



CK CREEK PASTURE FENCE

PHILLIPS COUNTY
MALTA FIELD OFFICE



DRAWING INDEX


CK CREEK PASTURE FENCE LOCATION

AUTOCAD NAME: CK CREEK PASTURE FENCE.dwg	MARK	REVISION	DATE	APPROVED
PROJECT NO: X				
DESIGN OFFICE: MALTA FIELD OFFICE				
RECOMMENDED BY DATE				
APPROVED BY DATE				


TITLE SHEET
CK CREEK PASTURE FENCE

MONTANA



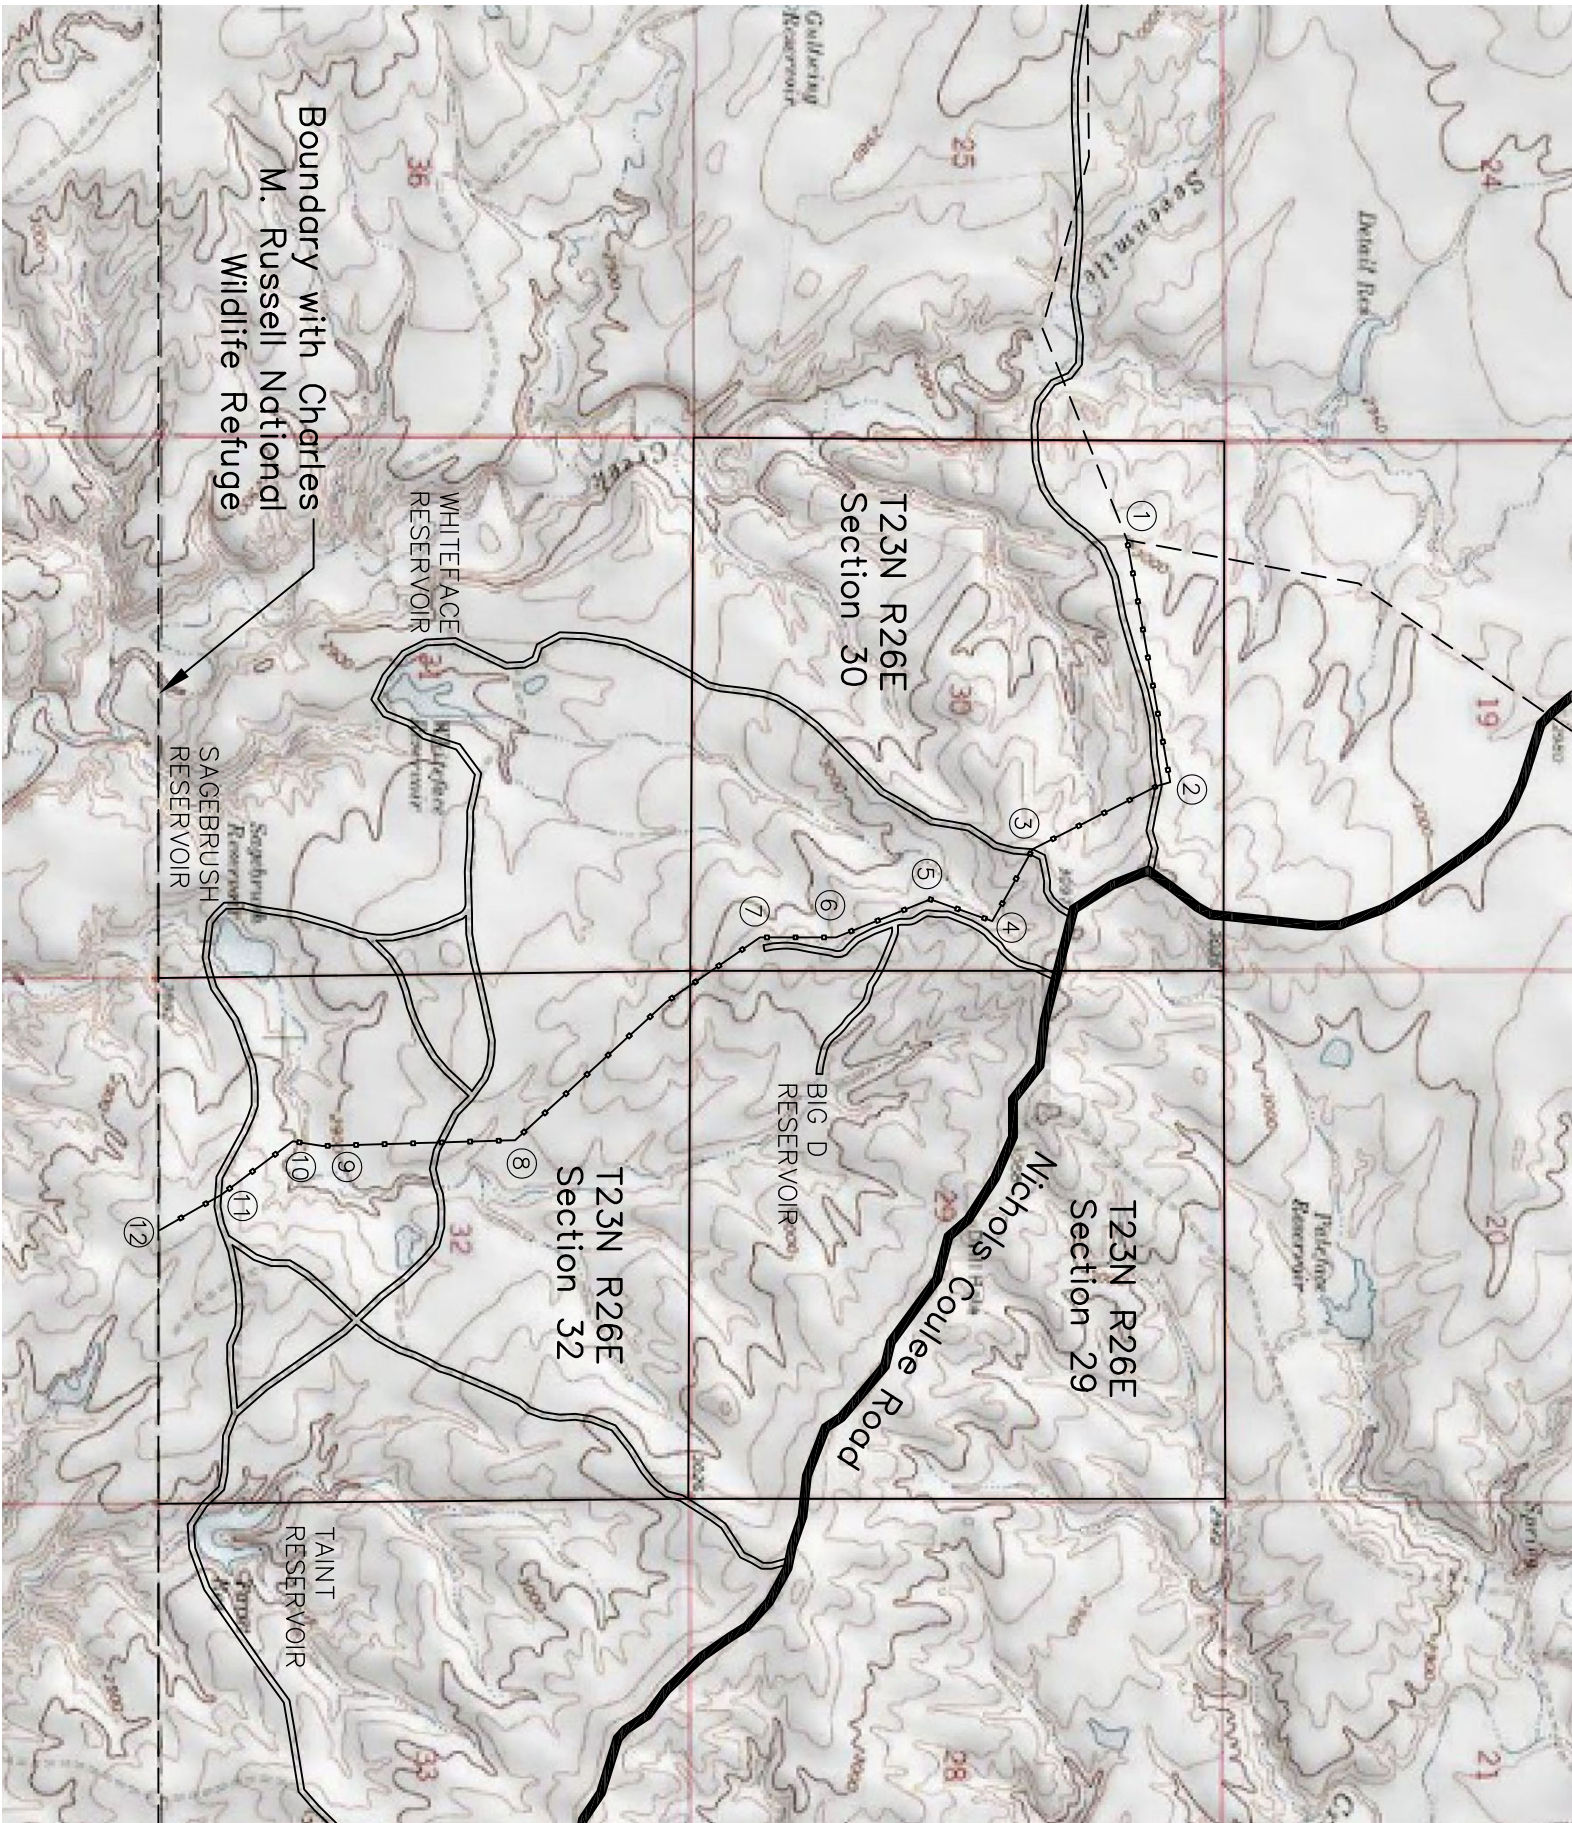

CK CREEK PASTURE FENCE LOCATION MAP

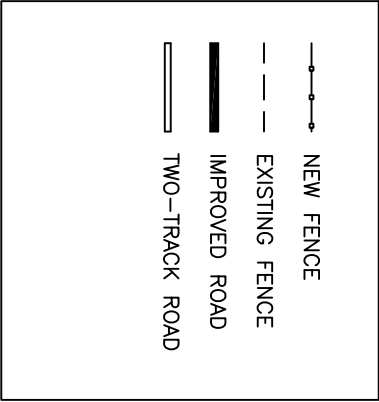

FENCE ALIGNMENT DATA *	
NUMBER	
LATITUDE	LONGITUDE
①	47.731549 -108.437459
②	47.732311 -108.427246
③	47.728860 -108.424750
④	47.727690 -108.421714
⑤	47.725950 -108.422622
⑥	47.723320 -108.421052
⑦	47.721229 -108.421022
⑧	47.713387 -108.412870
⑨	47.709425 -108.412657
⑩	47.708467 -108.412815
⑪	47.706679 -108.410729
⑫	47.705065 -108.409374

* Note: Latitude and Longitude coordinates are approximate. Precise field locations will be staked by the Government.




UNITED STATES DEPARTMENT OF THE INTERIOR
BUREAU OF LAND MANAGEMENT

LOCATION MAP CK CREEK PASTURE FENCE

MALTA FIELD OFFICE

MONTANA

AUTOCAD NAME: CK CREEK PASTURE FENCE.dwg	MARK	REVISION	DATE	APPROVED
DESIGN OFFICE: MALTA FIELD OFFICE				
DESIGNED BY: RS			DATE: 02/11/26	
DRAWN BY: RS			DATE: 02/11/26	
CHECKED BY: X			DATE: X	
APPROVED BY: X			DATE: X	

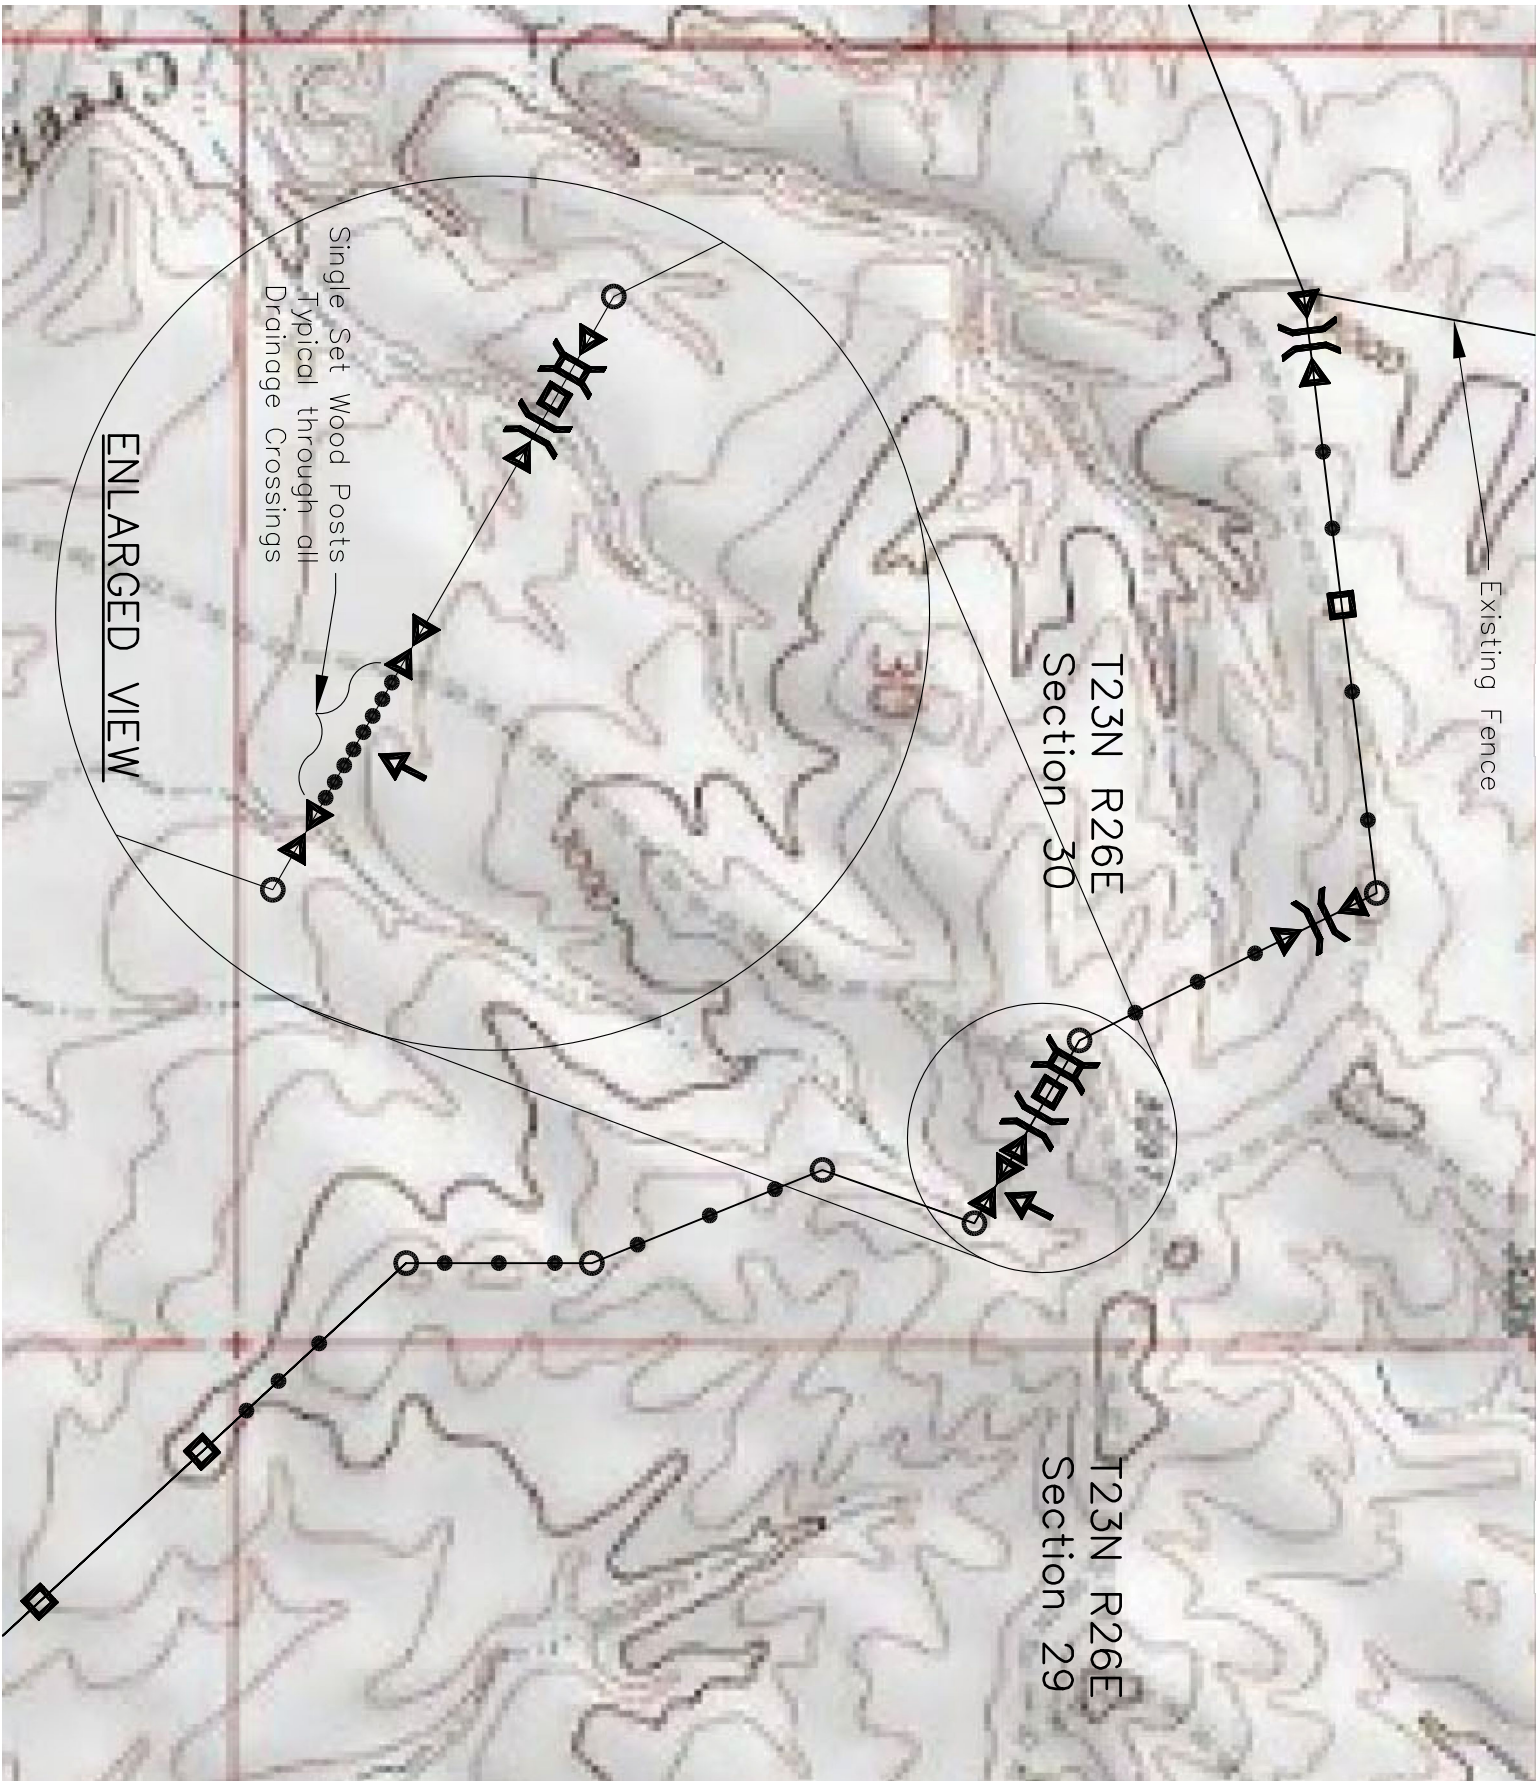

SECTIONS 29 & 30 FENCE PLAN



—	BARBED WIRE FENCE
▲	END PANEL
◻	STRESS PANEL
○	CORNER PANEL
•	WIRE GATE
⋈	SINGLE SET POST
⬆	DRAINAGE CROSSING
⋈	CATTLE GUARD

QUANTITIES AT SECTIONS 29 & 30			
No.	PAY ITEM DESCRIPTION	QTY	UNIT
02834(9)	3 POST CORNER PANEL	6	EA
02834(5)	END PANEL	10	EA
02834(6)	3 POST STRESS PANEL	2	EA
02834(22)	GATE	3	EA
02836(1)	DRAINAGE CROSSING	14	ROD
02834(30)	SINGLE SET WOOD POST	30	EA
02834(2)	4 WIRE FENCE	540	ROD
02881(1)	CATTLE GUARD	1	EA



SECTIONS 29 & 30 FENCE PLAN
CK CREEK PASTURE FENCE

UNITED STATES DEPARTMENT OF THE INTERIOR
BUREAU OF LAND MANAGEMENT

MALTA FIELD OFFICE

MONTANA


APPROVED

DATE

REVISION


MARK

AUTOCAD NAME: CK CREEK PASTURE FENCE.dwg	
DESIGN OFFICE: MALTA FIELD OFFICE	
DESIGNED BY: RS	DATE: 02/12/26
DRAWN BY: RS	DATE: 02/12/26
CHECKED BY: X	DATE: X
APPROVED BY: X	DATE: X

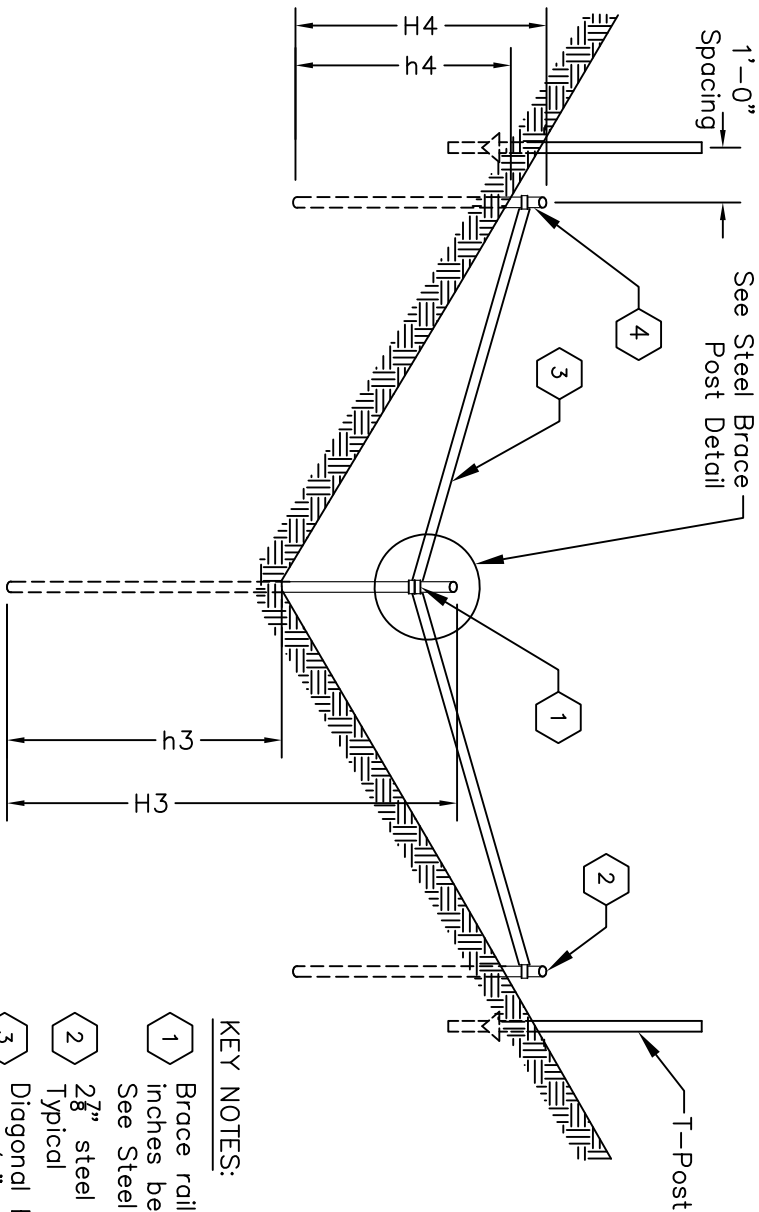

KEY NOTES:

- 1 Brace rail bands attach 4 to 6 inches below top wire height See Steel Brace Post Detail
- 2 2⁷/₈" steel dome post cap Typical
- 3 Diagonal Brace Rail: 2-³/₈" diameter x 8' to 9.5' length
- 4 Brace Rail Band attach 3" maximum above ground surface Typical

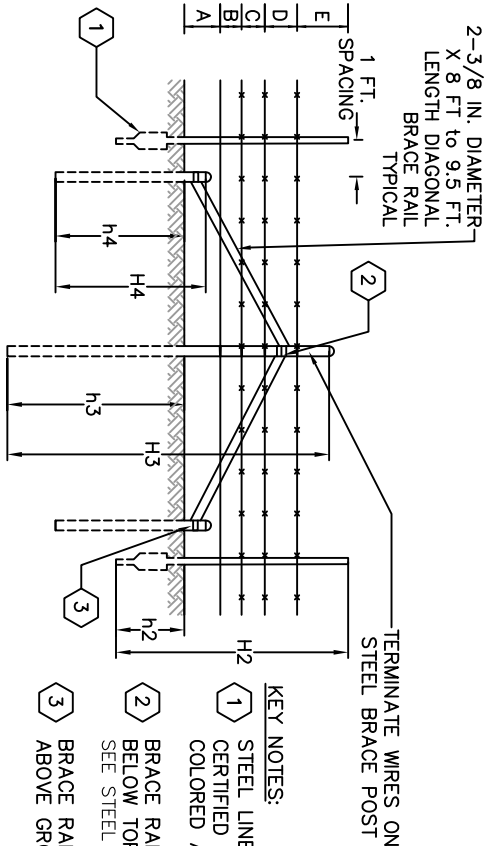

KEY NOTES:

- 1 STEEL LINE POST SHALL BE 5-1/2 FT. CERTIFIED 1.33 LBS/FT MINIMUM AND COLORED ACCORDING TO SPECIFICATIONS
- 2 BRACE RAIL BANDS ATTACH 4 TO 6 IN. BELOW TOP WIRE HEIGHT SEE STEEL BRACE POST DETAIL
- 3 BRACE RAIL BAND ATTACH 3 IN. MAXIMUM ABOVE GROUND SURFACE

3-POST STRESS PANEL

Not To Scale


- NOTES:
1. Number of wires, type of wire, and wire spacing same as for fence.
 2. If the 3 post corner is being used in line to form a tee, braces in both directions are required in the continuous panel.

3-POST CORNER PANEL

Not To Scale

GENERAL NOTES:

See Work Data Sheet for Fence and Gate dimensions.

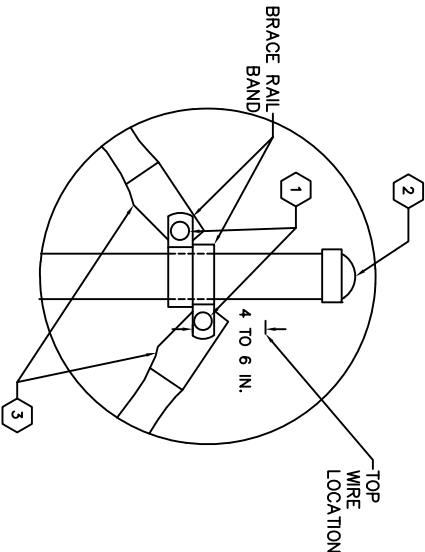

KEY NOTES:


- 1 ³/₈" galvanized grade 5 carriage bolt Typical
- 2 2⁷/₈" steel dome post cap Typical
- 3 Weld on ¹/₄" plate, or flatten approx. 1¹/₂" on both ends of the brace rail and drill/punch a hole in the plate or flattened area for ³/₈" bolt

GENERAL NOTE:

Number of wires, type of wire, and wire spacing same as that shown on Line Panels Detail.


STEEL BRACE POST DETAIL

Not To Scale

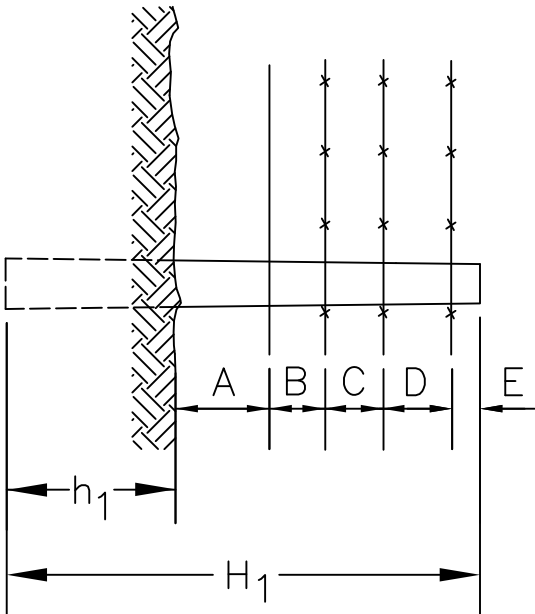

SINGLE SET WOOD POST

Not To Scale

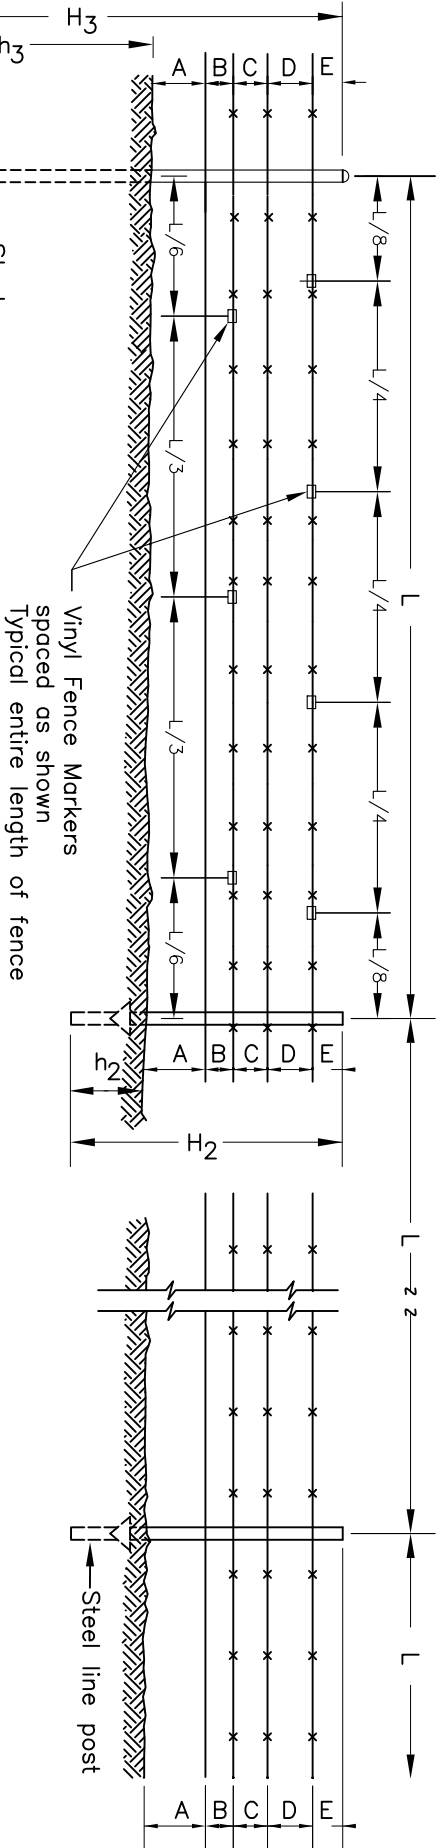

LINE PANELS

Not To Scale

SAFETY FIRST CALL BEFORE DIGGING 1-800-424-5555 Montana811.org




UNITED STATES DEPARTMENT OF THE INTERIOR
BUREAU OF LAND MANAGEMENT
FENCE DETAILS No. 1
CK CREEK PASTURE FENCE

MALTA FIELD OFFICE

MONTANA


APPROVED	DATE	REVISION	MARK	AUTOCAD NAME: CK CREEK PASTURE FENCE.dwg
				DESIGN OFFICE: MALTA FIELD OFFICE
				DESIGNED BY: RS DATE: 02/12/26
				DRAWN BY: RS DATE: 02/12/26
				CHECKED BY: X DATE: X
				APPROVED BY: X DATE: X

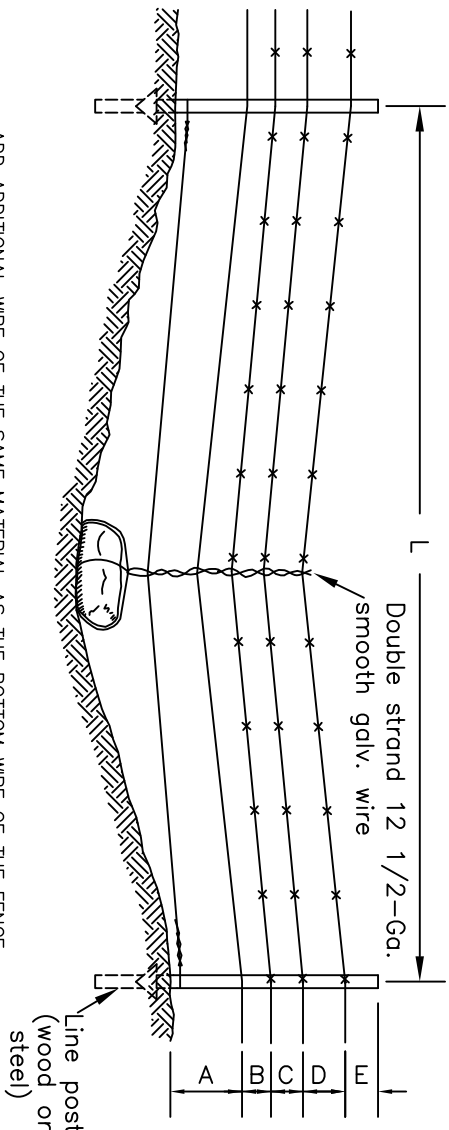

ADD ADDITIONAL WIRE OF THE SAME MATERIAL AS THE BOTTOM WIRE OF THE FENCE AND A ROCK DEADMAN ARE REQUIRED WHEN THE DISTANCE BETWEEN THE BOTTOM WIRE AND THE GROUND EXCEEDS 20 INCHES. NOTE ROCKS SHALL WEIGHT A MINIMUM OF 50 LBS AND SECURELY FASTENED TO THE WIRE.

PANEL AT MINOR DEPRESSION


Not To Scale ROCK DEADMAN

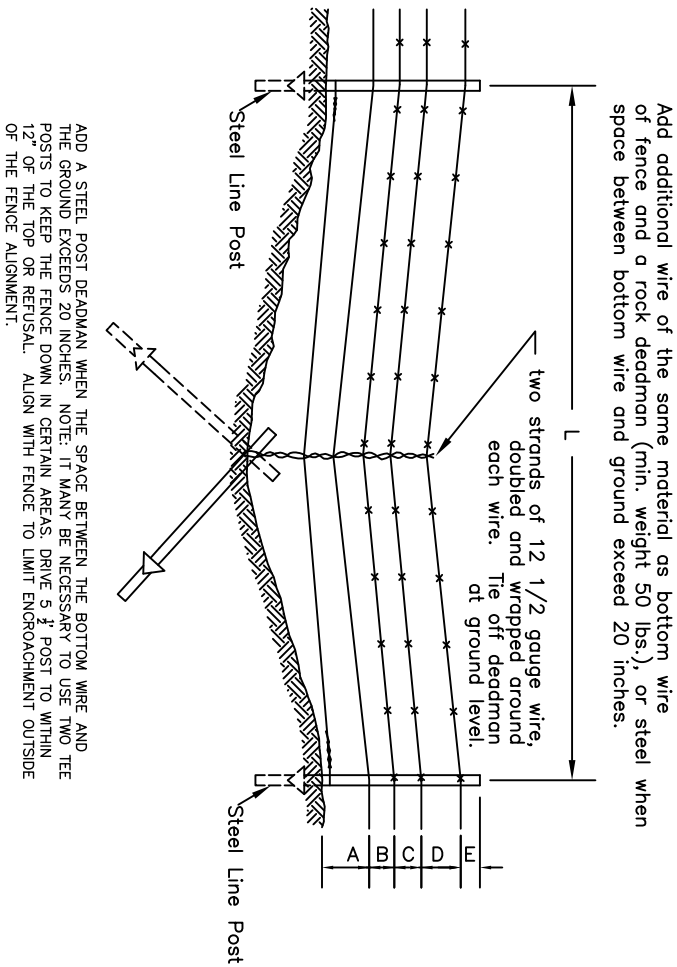

ADD A STEEL POST DEADMAN WHEN THE SPACE BETWEEN THE BOTTOM WIRE AND THE GROUND EXCEEDS 20 INCHES. NOTE, IT MANY BE NECESSARY TO USE TWO TEE POSTS TO KEEP THE FENCE DOWN IN CERTAIN AREAS. DRIVE 5 1/2" POST TO WITHIN 12" OF THE TOP OR REFUSAL. ALIGN WITH FENCE TO LIMIT ENCROACHMENT OUTSIDE OF THE FENCE ALIGNMENT.

PANEL AT MINOR DEPRESSION

Not To Scale STEEL POST DEADMAN

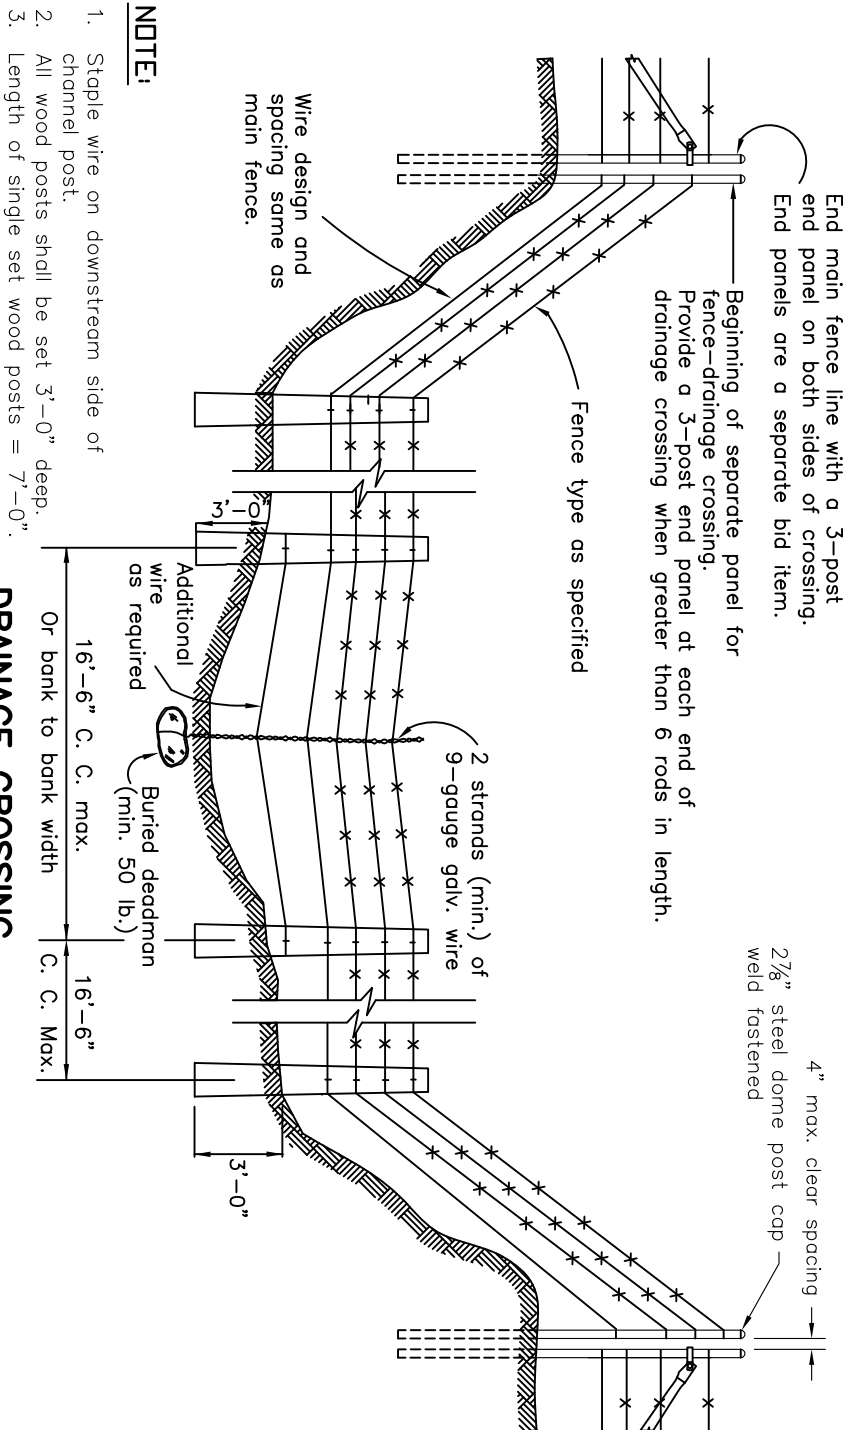


NOTE:

1. Staple wire on downstream side of channel post.
2. All wood posts shall be set 3'-0" deep.
3. Length of single set wood posts = 7'-0".

DRAINAGE CROSSING

Not To Scale

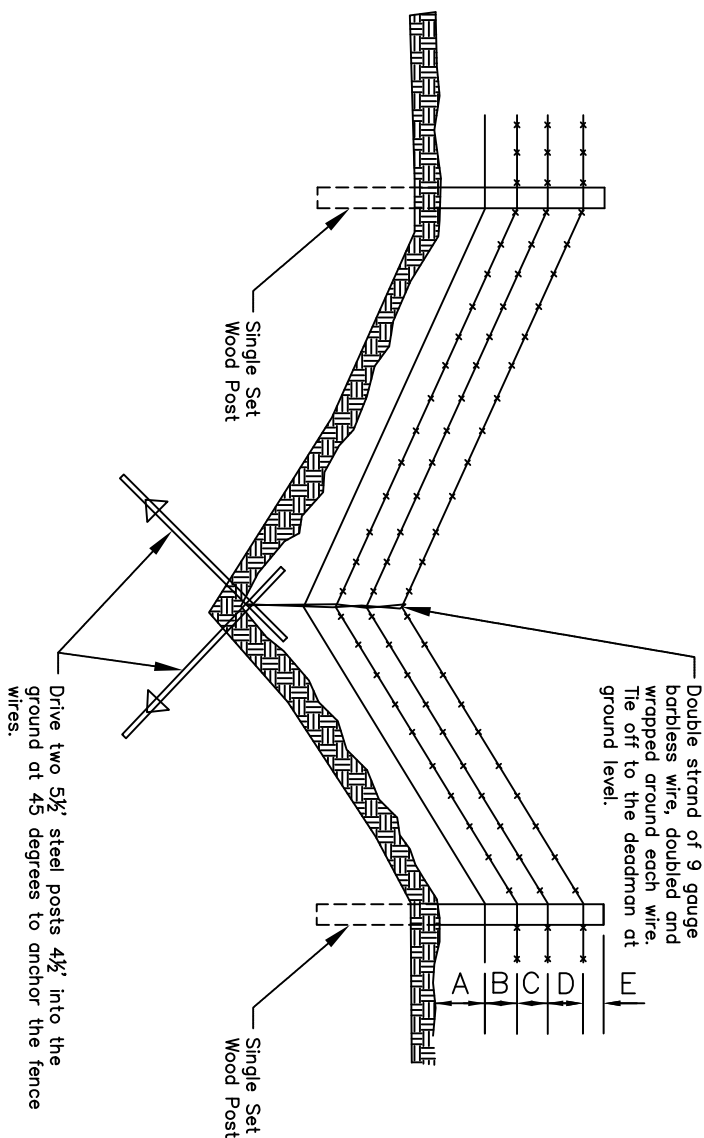

PANEL W/ DEADMAN AT SEVERE DEPRESSION

Not To Scale




UNITED STATES DEPARTMENT OF THE INTERIOR
BUREAU OF LAND MANAGEMENT

FENCE DETAILS No. 2
CK CREEK PASTURE FENCE

MALTA FIELD OFFICE

MONTANA

APPROVED	DATE	REVISION	MARK	AUTOCAD NAME: CK CREEK PASTURE FENCE.dwg
				DESIGN OFFICE: MALTA FIELD OFFICE
				DESIGNED BY: RS DATE: 02/12/26
				DRAWN BY: RS DATE: 2/12/26
				CHECKED BY: X DATE: X
				APPROVED BY: X DATE: X

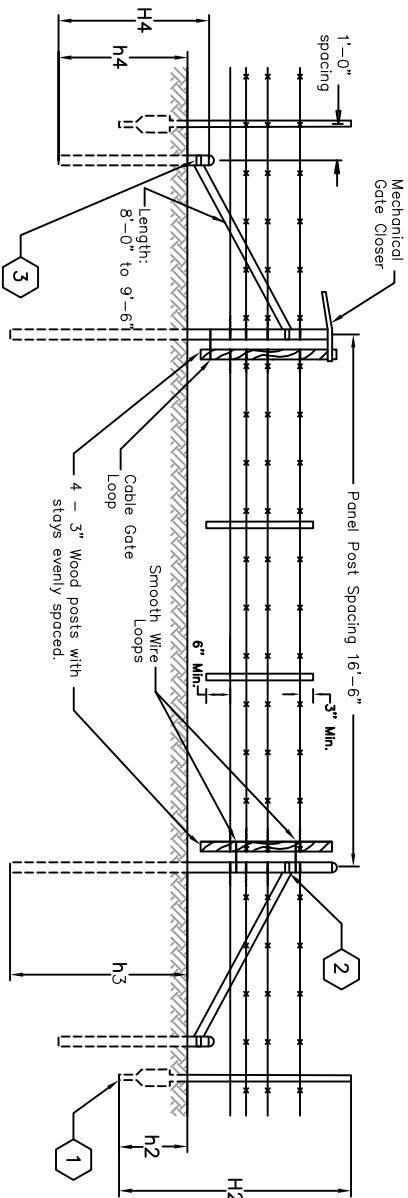

4--WIRE GATE


Not To Scale

KEY NOTES:

1. STEEL LINE POST SHALL BE 5-1/2 FT. CERTIFIED 1.33 LBS/FT MINIMUM AND COLORED TO MATCH SPECIFICATIONS
2. BRACE RAIL BANDS ATTACH 4 TO 6 IN. BELOW TOP WIRE HEIGHT
3. BRACE RAIL BAND ATTACH 3 IN. MAXIMUM ABOVE GROUND SURFACE

NOTES:

1. Drill stem mechanical gate closer construction based on design in specifications and drawings. Gate closer shall provide cover for the top of the steel brace post to seal water out.
2. Construct an end or stress panel on each side of gate as required in the drawings and specifications.
3. All steel brace posts shall be capped.

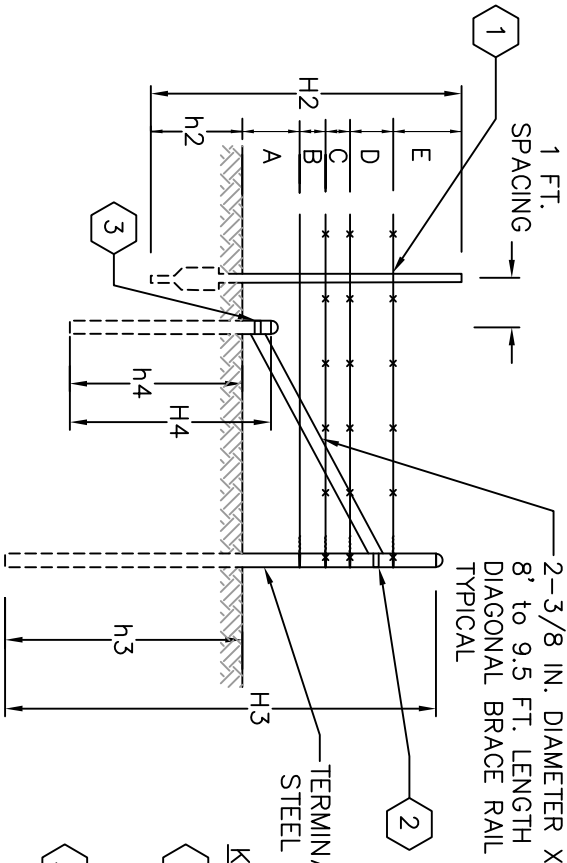


KEY NOTES:


1. STEEL LINE POST SHALL BE 5-1/2 FT. CERTIFIED 1.33 LBS/FT MINIMUM AND COLORED ACCORDING TO SPECIFICATIONS
2. BRACE RAIL BANDS ATTACH 4 TO 6 IN. BELOW TOP WIRE HEIGHT
SEE STEEL BRACE POST DETAIL SHEET 5 (SIMILAR)
3. BRACE RAIL BAND ATTACH 3 IN. MAXIMUM ABOVE GROUND SURFACE

2-POST END PANEL


Not To Scale

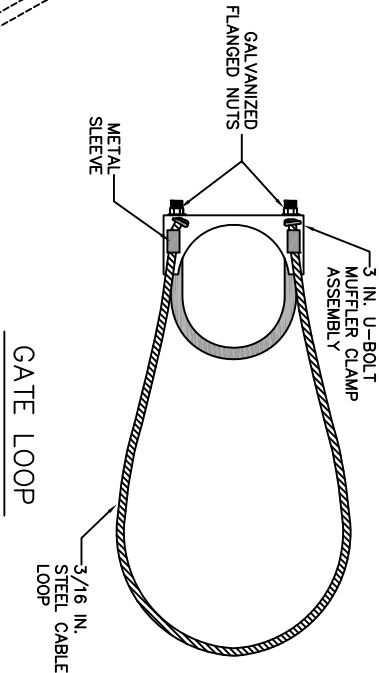


GATE LOOP

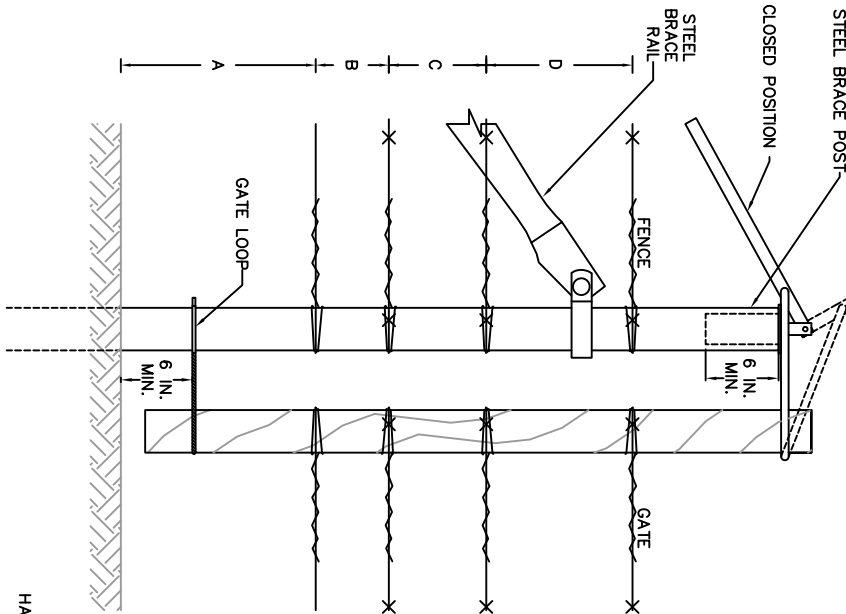

- NOTE:
1. STEM ON GATE CLOSER SHALL BE INSERTED SECURELY INSIDE AND FLUSH WITH THE TOP OF THE STEEL BRACE POST
 2. GATE CLOSER SHALL PROVIDE A COVER FOR THE STEEL BRACE POST TOP
 3. GATE SHALL BE A HAVE FOUR WIRES
 4. DRAWING IS NOT DRAWN TO SCALE

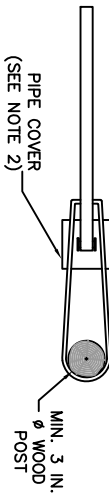

TOP VIEW

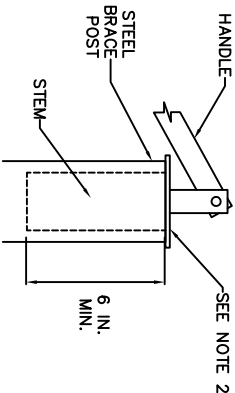

SIDE VIEW

MECHANICAL GATE CLOSER DETAIL

Not To Scale

SAFETY FIRST CALL BEFORE DIGGING 1-800-424-5555 Montana811.org



UNITED STATES DEPARTMENT OF THE INTERIOR
BUREAU OF LAND MANAGEMENT

FENCE DETAILS No. 3

CK CREEK PASTURE FENCE

MALTA FIELD OFFICE

MONTANA

APPROVED	DATE	REVISION	MARK	AUTOCAD NAME: CK CREEK PASTURE FENCE.dwg
				DESIGN OFFICE: MALTA FIELD OFFICE
				DESIGNED BY: RS DATE: 02/12/26
				DRAWN BY: RS DATE: 02/12/26
				CHECKED BY: X DATE: X
				APPROVED BY: X DATE: X

