


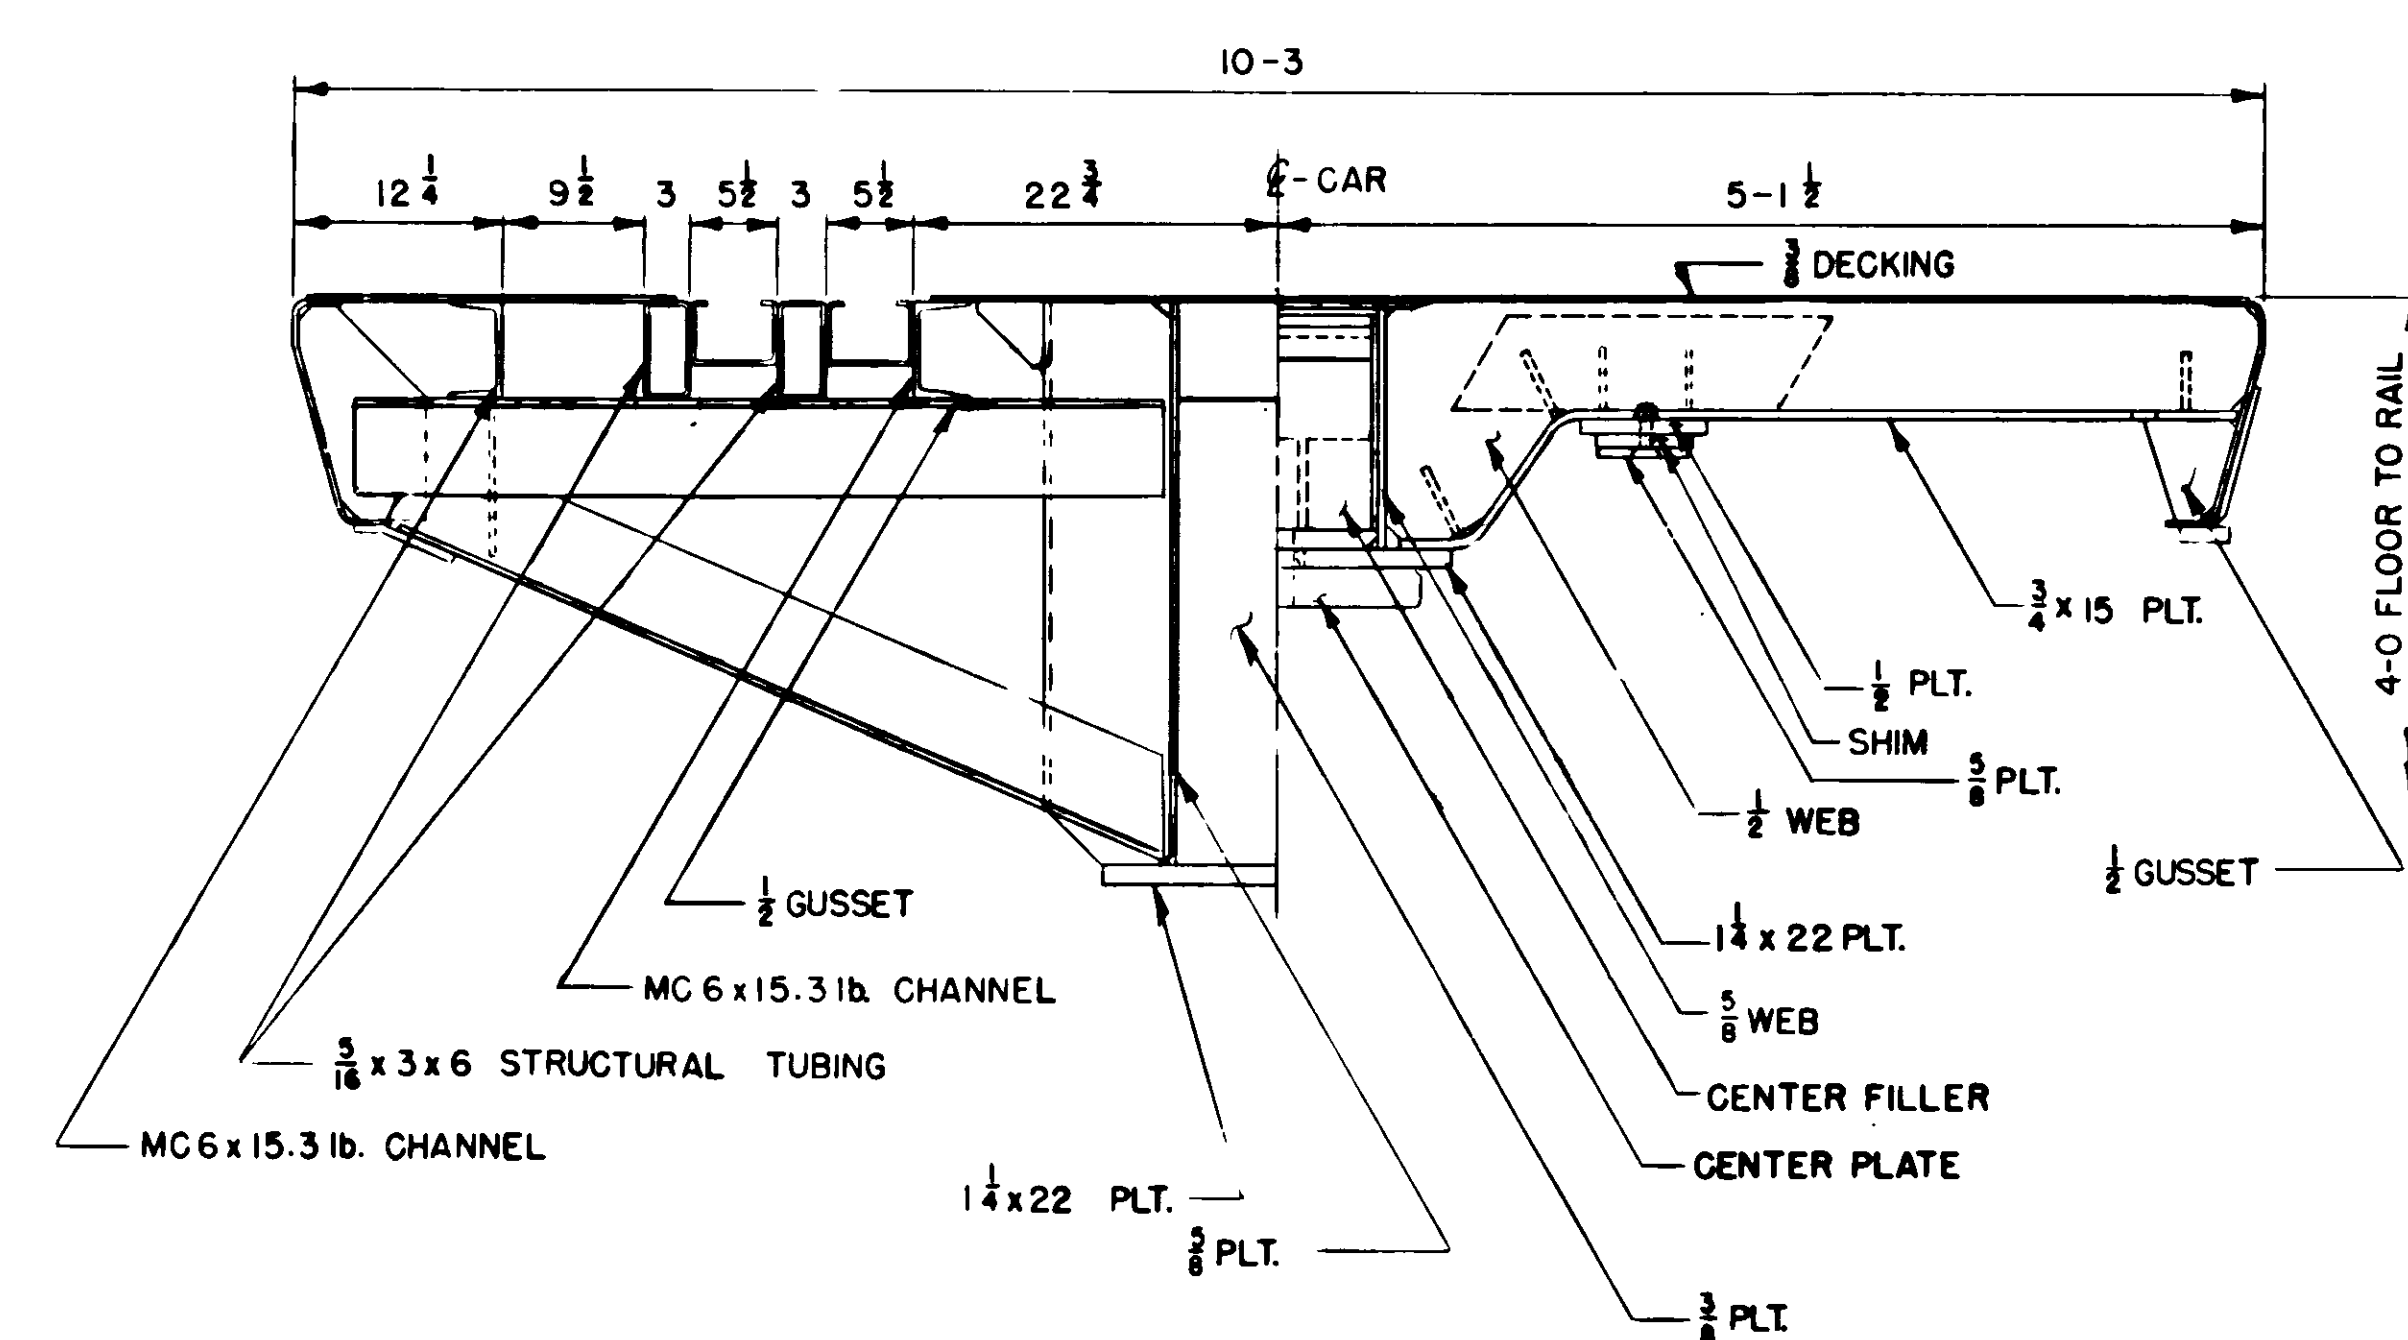


 


SECTIONS THRU CROSSBEARER AND BOLSTER
SCALE: 1/4" = 1'-0"

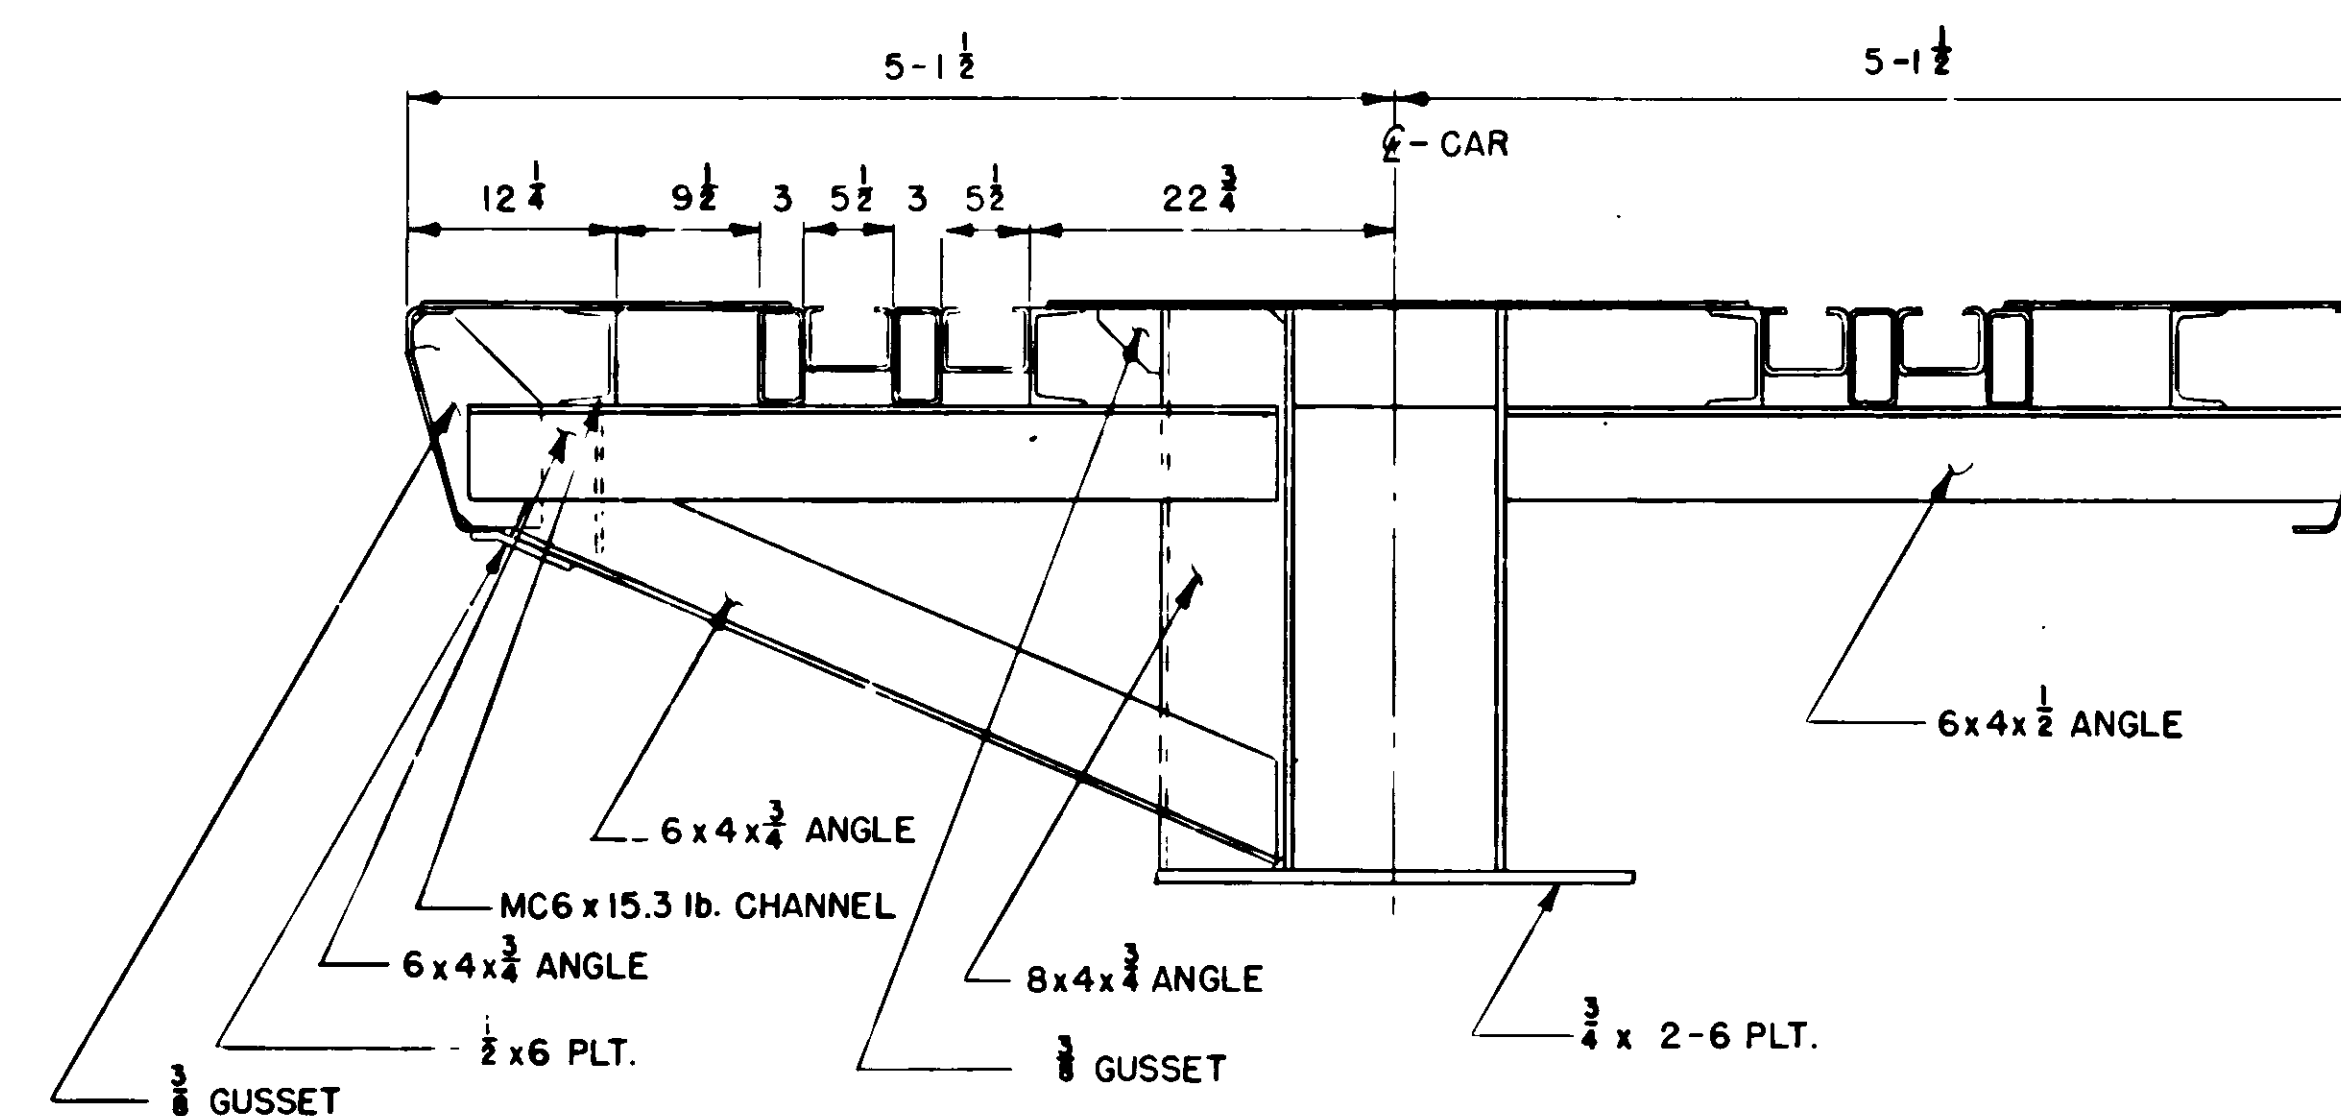

SECTION THRU CROSSBEARER NEXT
TO CENTER LINE OF CAR
SCALE: 1/4" = 1'-0"

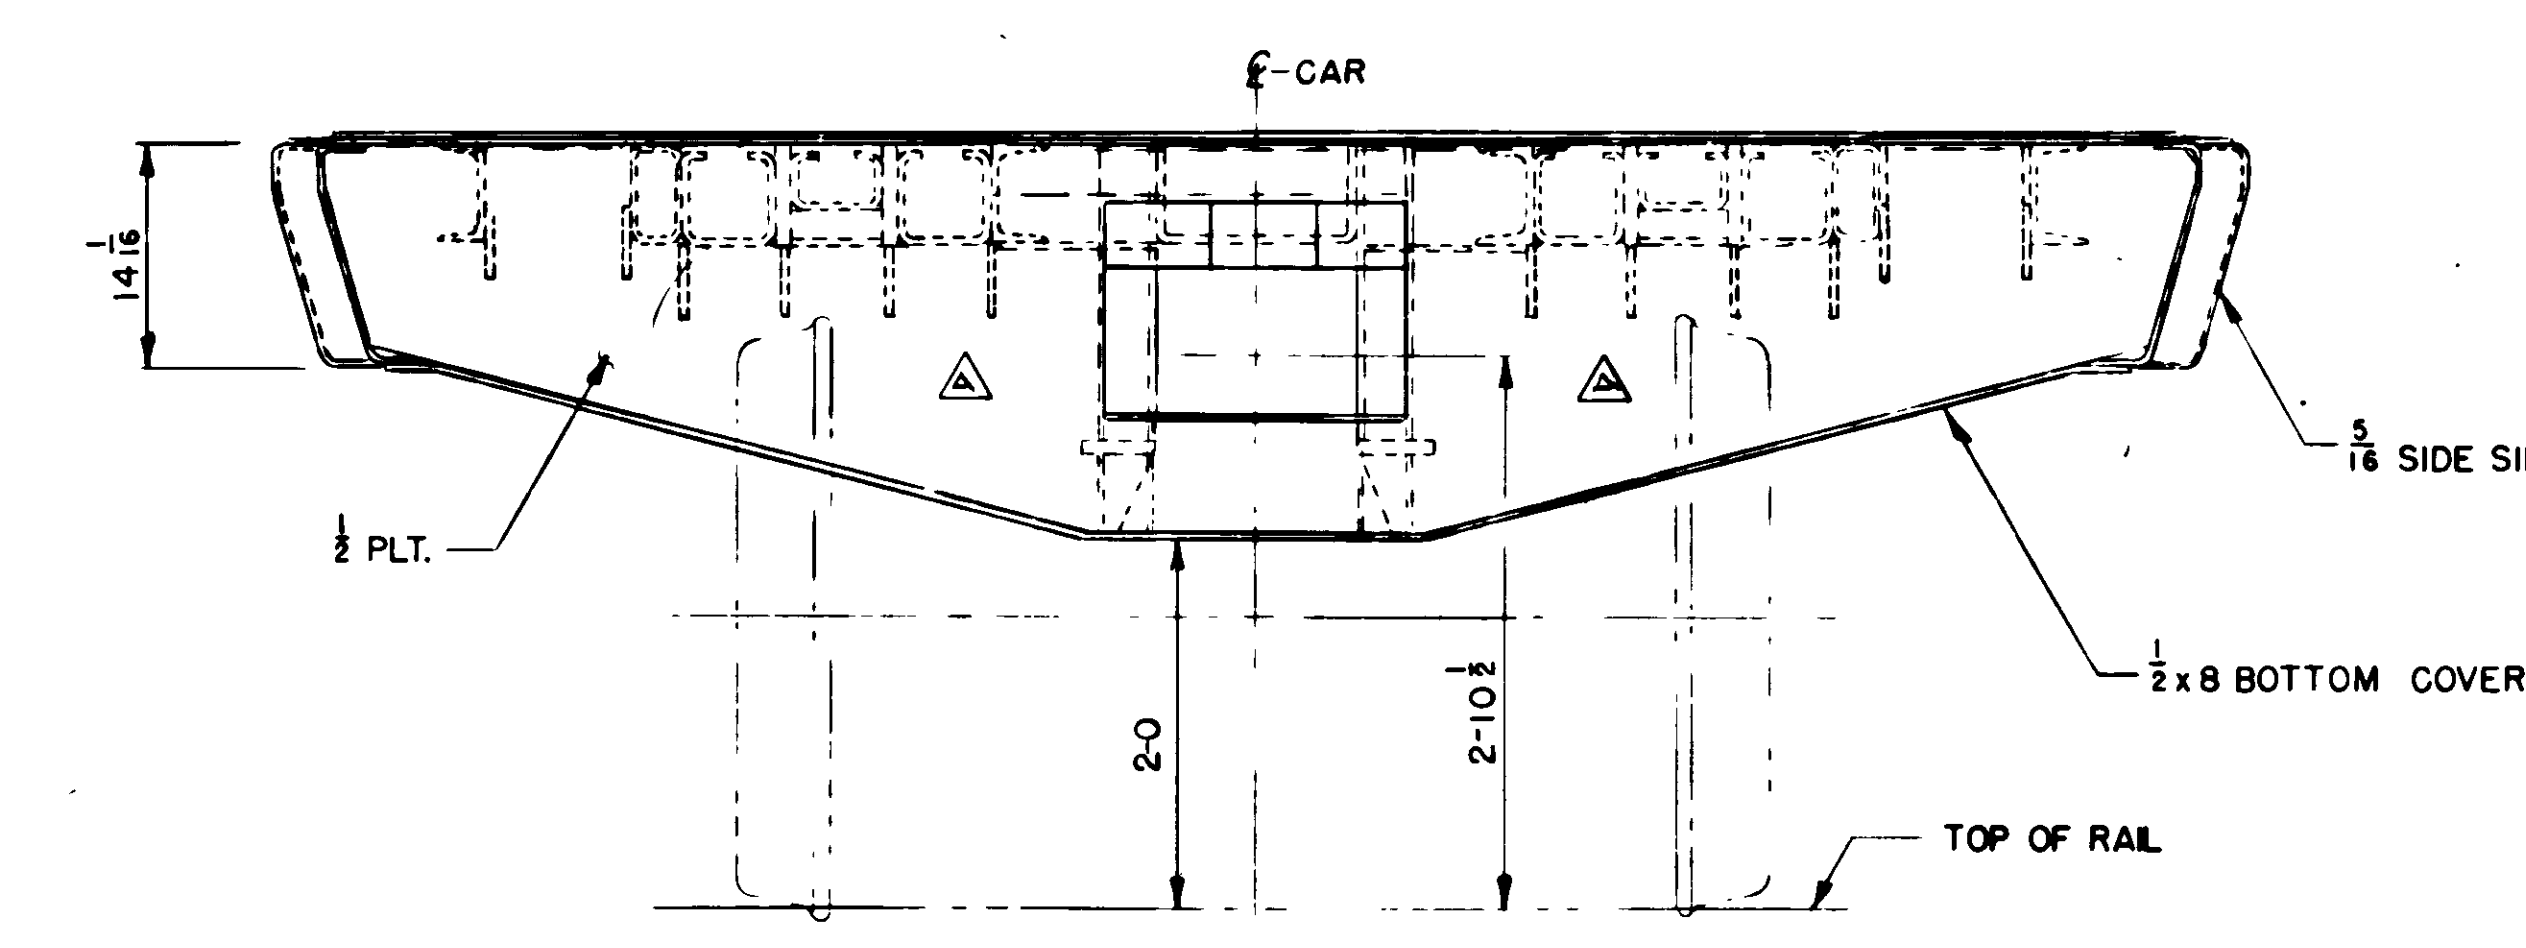

END VIEW
SCALE: 1/4" = 1'-0"

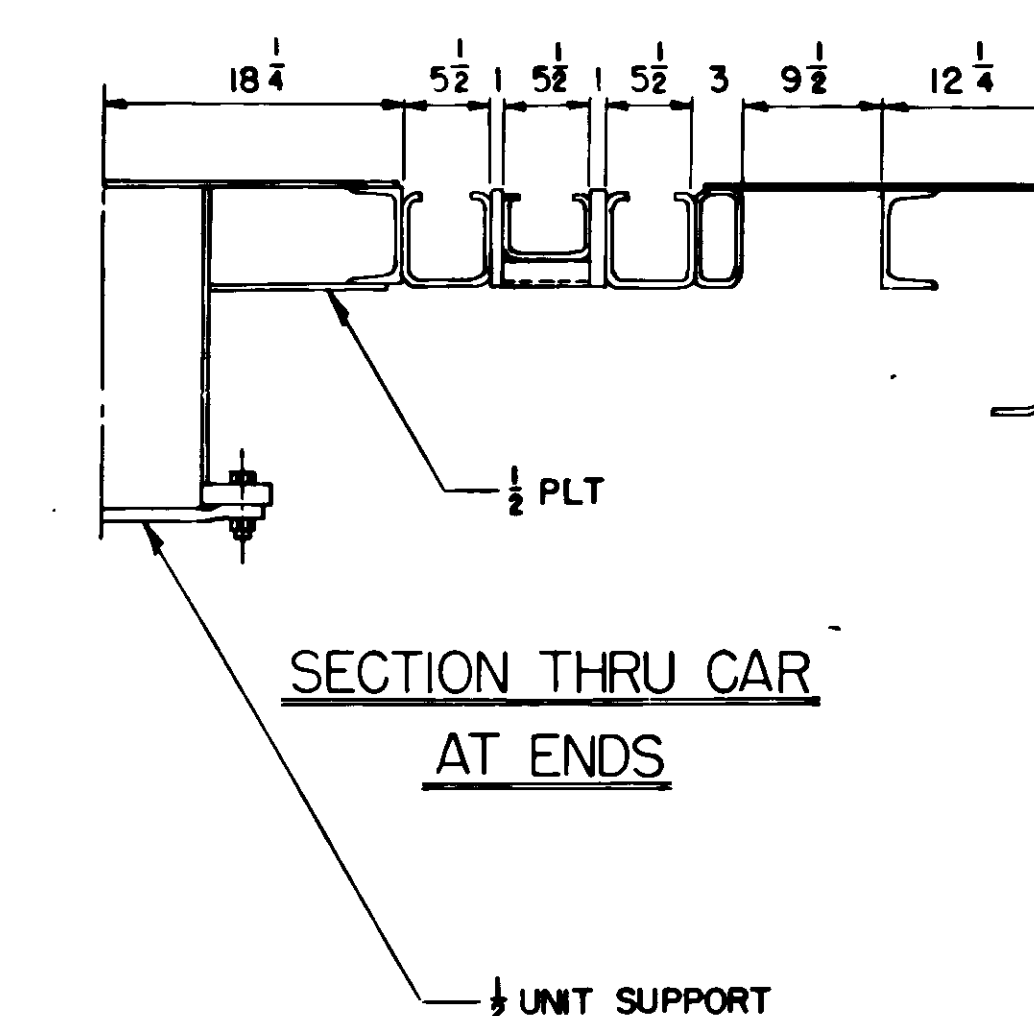

SECTION THRU CAR
AT ENDS

LIMITED RIGHTS LEGEND
CONTRACT NO. DBA-409-80-5393
CONTRACTOR FGE CO.
EXPLANATION OF LIMITED RIGHTS DATA
IDENTIFICATION METHOD USED
ANY ITEM MARKED WITH "P" IS
RESTRICTED

REV	INT	DATE	DESCRIPTION
1			REVISED DIMENSION LINE
2			REMOVED SPACE TO CLEAR
3			ADDED RELATIVE TO REWORKED
4			CHANGED TO CORRECT DIMENSIONS
FGE Fruit Growers Express Company			
TITLE: GENERAL ARRANGEMENT			
68'-0" 140 TON FLAT CAR			
DR	SK	DATE	SCALE
JAL	J.A.V.	12-8-80	1/16" = 1'-0"
106-0001			