



ROLLING DIP DETAIL

NO SCALE

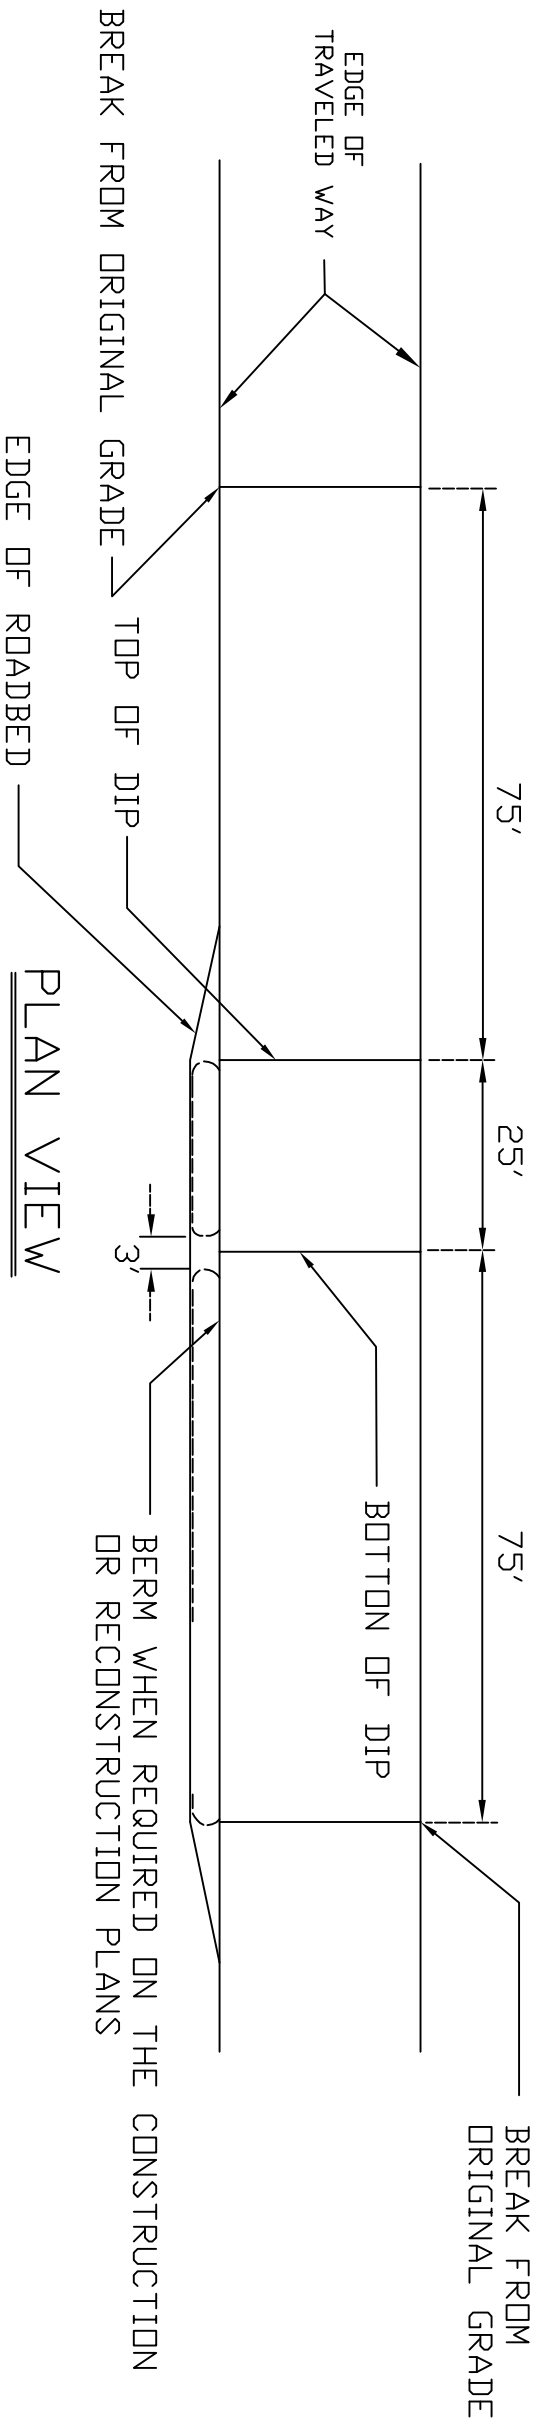

PROFILE VIEW

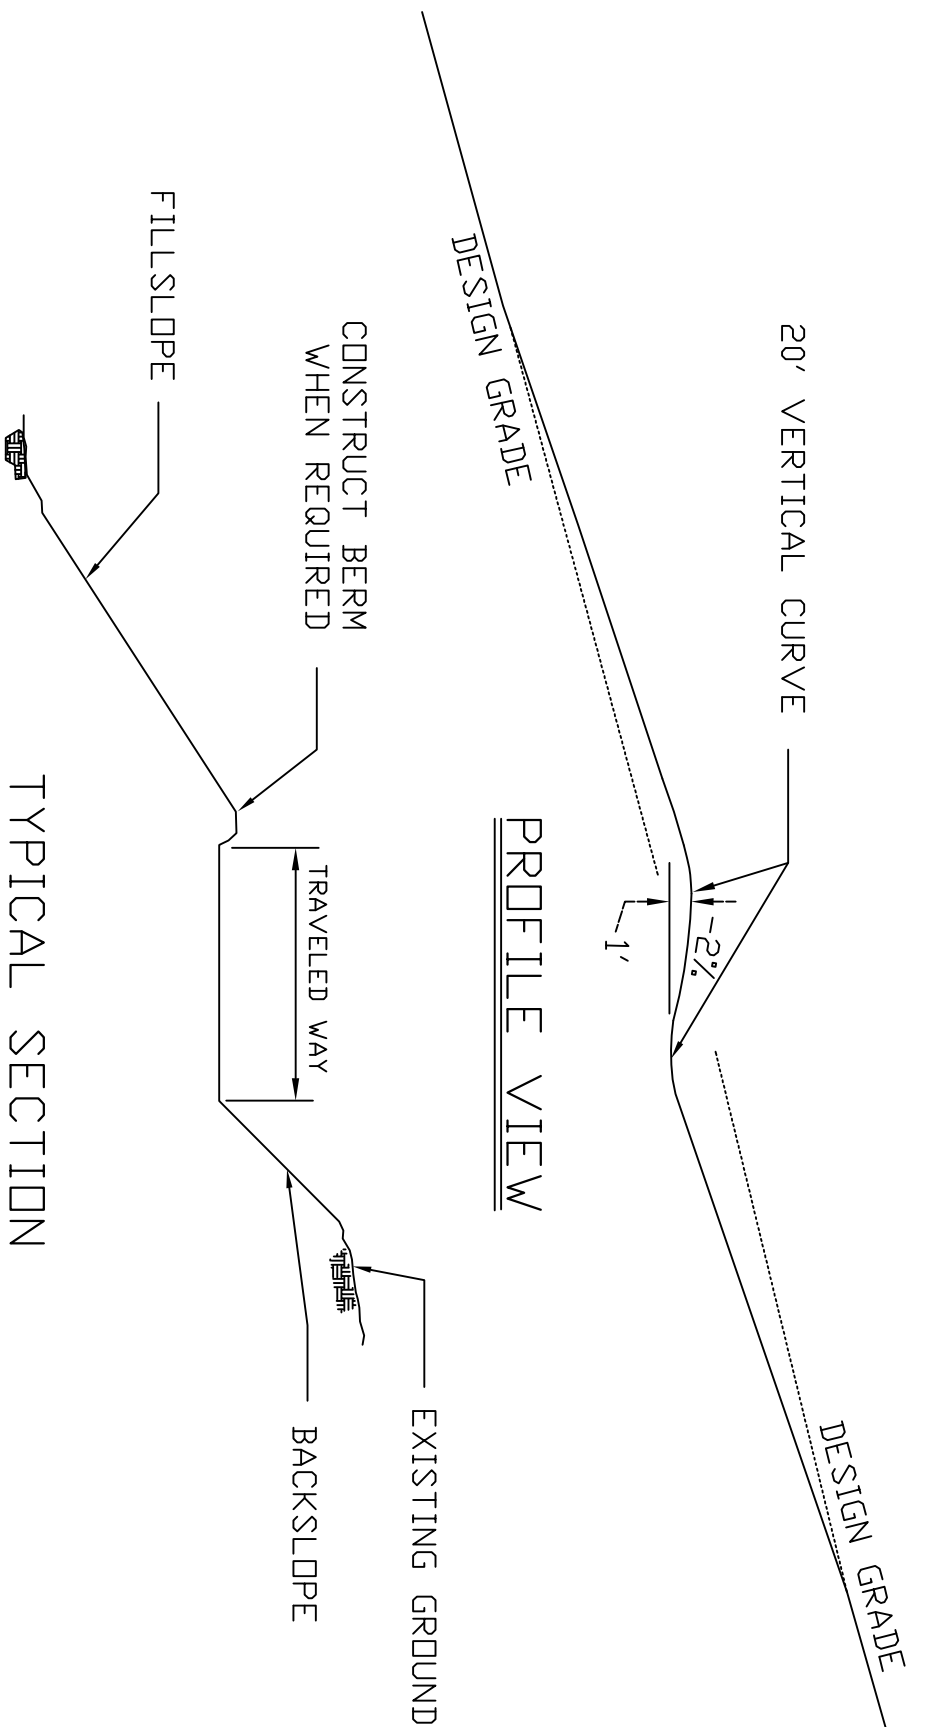

TYPICAL SECTION

ROLLING DIP DETAIL		
PROJECT NAME	SHEET NUMBER	OF SHEETS