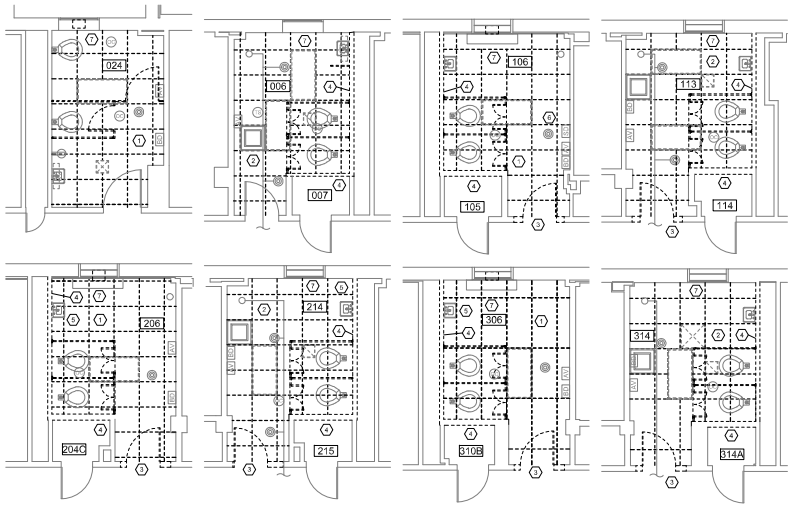

1 ARCHITECTURAL AND REFLECTIVE CEILING DEMO PLAN

1/4" = 1' - 0"

DEMO KEYED NOTES

1 DEMO CEILING TILE AND GRID. DOCUMENT EXISTING GRID LOCATION AND ELEVATION. NEW GRID TO BE SIMILAR. SUPPORT LIGHTING FIXTURES TO BE DEMO'D UNTIL REPLACEMENT.
2 DEMO CEILING TILE AND GRID. DOCUMENT EXISTING GRID ELEVATION. NEW GRID TO BE SIMILAR. SUPPORT LIGHTING FIXTURES TO BE DEMO'D. SUPPORT HVAC UNIT TO BE RE-USED.
3 DEMO DOOR AND ASSOCIATED HARDWARE INCLUDING FRAME. DEMO WALL AS REQUIRED FOR NEW CASED OPENING TO BE CENTERED IN NEW RECESS.
4 DEMO WALL INCLUDING CLAY TILE STRUCTURE.
5 DEMO SHELF AND ALL ASSOCIATED MOUNTING HARDWARE.
6 DEMO SANITARY NAPKIN DISPENSER
7 STRIP PAINT FROM WINDOW SILL USING LEAD PAINT PROCEDURES. SEE SPECIFICATIONS SECTION 02 83 33.13

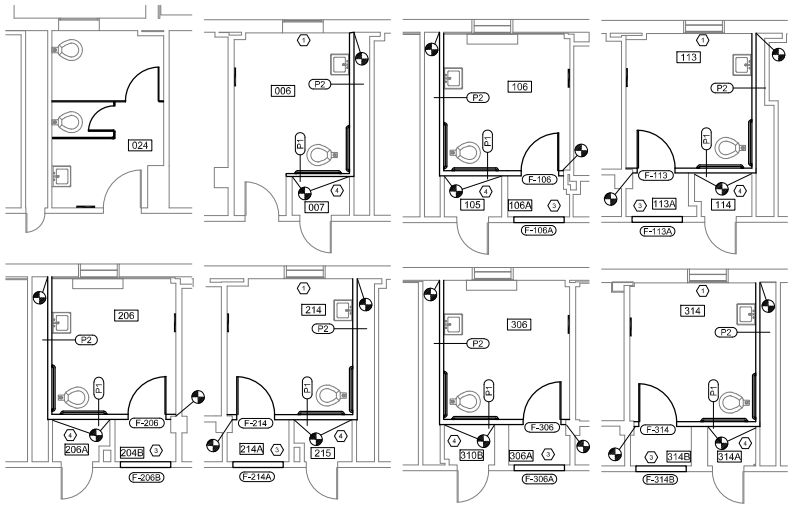

2 ARCHITECTURAL PLAN

1/4" = 1' - 0"

KEYED NOTES

1 RE-GLAZE UPPER PANE TO MATCH WINDOW IN ROOM 316.
2 REPLACE WALL MOUNTED COVER PLATES
3 CENTER OPENING TO NEW RECESS. REFERENCE DET 3 / A1102 FOR NEW TO EXISTING FLOOR TRANSITION.
4 EXTEND EXISTING WALL AS NEEDED TO MEET NEW WALL AND FILL GAPS. LOCATE NEW WALL TO MEET ADA REQUIREMENTS.

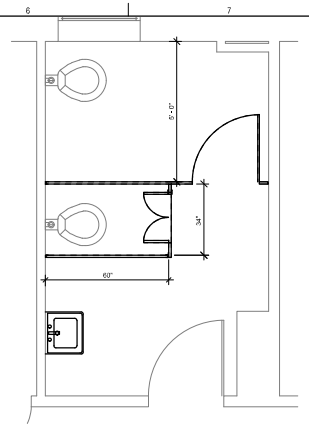

3 ROOM 024 PARTITIONS

SCALE: ¼" = 1' - 0"

LEGEND

- RECESSED LIGHT FIXTURE
- WALL MOUNTED LIGHT FIXTURE
- OCCUPANCY SENSOR
- SPRINKLER HEAD
- RETURN / EXHAUST GRILL / REGISTER
- SUPPLY DIFFUSER
- 2'x2' ACOUSTICAL TILE CEILING
- FIRE ALARM
- WALL MOUNTED WATER CLOSET
- FLOOR MOUNTED WATER CLOSET
- BIOHAZARDOUS DISPOSAL
- LAVATORY
- NEW TO EXISTING
- SINGLE POLE SWITCH
- SANITARY NAPKIN DISPENSER

DOOR & FRAME DIMENSIONS

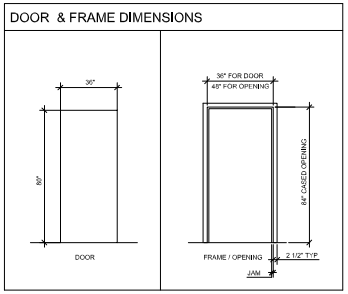

OPENING SCHEDULE

NUMBER	TYPE	WIDTH	HEIGHT	FRAME MATERIAL	DOOR MATERIAL	COMMENTS
F-106A	DOOR	3' - 0"	6' - 8"	STEEL	WOOD	MATCH EXISTING, REUSE HARDWARE
F-106A	CASED OPENING	4' - 0"	7' - 0"	STEEL	N/A	
F-113	DOOR	3' - 0"	6' - 8"	STEEL	WOOD	MATCH EXISTING, REUSE HARDWARE
F-113A	CASED OPENING	4' - 0"	7' - 0"	STEEL	N/A	
F-206	DOOR	3' - 0"	6' - 8"	STEEL	WOOD	MATCH EXISTING, REUSE HARDWARE
F-206B	CASED OPENING	4' - 0"	7' - 0"	STEEL	N/A	
F-214	DOOR	3' - 0"	6' - 8"	STEEL	WOOD	MATCH EXISTING, REUSE HARDWARE
F-214A	CASED OPENING	4' - 0"	7' - 0"	STEEL	N/A	
F-306	DOOR	3' - 0"	6' - 8"	STEEL	WOOD	MATCH EXISTING, REUSE HARDWARE
F-306A	CASED OPENING	4' - 0"	7' - 0"	STEEL	N/A	
F-314	DOOR	3' - 0"	6' - 8"	STEEL	WOOD	MATCH EXISTING, REUSE HARDWARE
F-314B	CASED OPENING	4' - 0"	7' - 0"	STEEL	N/A	

DEMOLITION GENERAL NOTES

1 REMOVE AND STORE ALL WALL MOUNTED RESTROOM ACCESSORIES INCLUDING ADA GRAB BARS, TOILET PAPER AND SOAP DISPENSERS, BIOHAZARD DISPOSAL ETC., TO BE RE-USED.
2 DEMO ALL ARTIFICIAL MARBLE PARTITIONS AND WALL COVERINGS. WALL TILE AND WALL PLASTER TO CLAY TILE.
3 DEMO ALL FLOOR TILE AND TILE MORTAR TO STRUCTURE.
4 REPAIR ANY DAMAGE TO ITEM THAT ARE TO REMAIN.
5 DEMOLITION ITEMS MAY NOT BE ALL INCLUSIVE. REMOVE ALL ITEMS REQUIRED FOR NEW CONSTRUCTION ACTIVITIES.
6 FIELD VERIFY EXTENT OF EXISTING CONDITIONS FOR DEMOLITION WITH THE CONSTRUCTION DOCUMENTS AND SCHEDULED CONSTRUCTION PRIOR TO DEMOLITION. DISCREPANCIES BETWEEN DESIGN AND EXISTING CONDITIONS SHALL BE BROUGHT TO THE ATTENTION OF THE COR.
7 ALL WALLS, INCLUDING FINISHES AND STRUCTURE, INDICATED BY DASHED LINES SHALL BE REMOVED.
8 AFTER REMOVAL OF EXISTING FLOOR, CONCRETE FLOOR SHALL BE GROUND SMOOTH BEFORE INSTALLATION OF NEW FINISH AT JUNCTIONS BETWEEN NEW AND EXISTING FLOORS, PROVIDE APPROPRIATE TRANSITION STRIP.
9 WHERE EXISTING DOORS, DOOR FRAMES, EQUIPMENT, PORTIONS OF WALLS ARE REQUIRED TO BE REMOVED FOR THE COMPLETION OF THE WORK, EXERCISE CAUTION TO AVOID DISRUPTING SURROUNDING MATERIALS.
9 MAINTAIN CLEAR EXIT PATHS DURING DEMOLITION AND CONSTRUCTION.
10 ANY ASBESTOS FOUND DURING DEMOLITION SHALL BE BROUGHT TO THE ATTENTION OF THE COR. CONTRACTOR SHALL ENCAPSULATE AND ABATE THE AFFECTED AREA PER THE DIRECTION OF A LICENSED PROFESSIONAL ENVIRONMENTAL CONTRACTOR.
11 ALL STRUCTURAL ELEMENTS SHALL BE PROTECTED DURING DEMOLITION.
12 ASBESTOS REPORT INCLUDED WITH SPECIFICATIONS. CONTRACTOR TO NOTIFY COR UPON EXPOSURE OF INSULATED PLUMBING. ASBESTOS TESTING WILL BE PERFORMED BY VA.

GENERAL NOTES

1 ALL INFECTION CONTROL CRITERIA AS SPECIFIED IN THE SECTION 01 35 26 SHALL BE ADHERED TO DURING ALL PHASES OF THE PROJECT.
2 EXCEPT FOR ADA DIMENSIONS, ALL DIMENSIONS ARE APPROXIMATE SIZES. ALL CONSTRUCTION DIMENSIONS SHALL BE FIELD VERIFIED BY CONTRACTOR PRIOR TO THE START OF CONSTRUCTION.
3 COORDINATE MOUNTING LOCATIONS OF ALL WALL MOUNTED DEVICES AND/OR EQUIPMENT IN ORDER TO ELIMINATE CONFLICTS.
4 CONTRACTOR SHALL PROVIDE AND INSTALL ALL NECESSARY BLOCKING/ANCHORAGE FOR ALL WALL MOUNTED EQUIPMENT AND ACCESSORIES.
5 ALL ALARMS WILL BE KEPT CONNECTED AND IN WORKING ORDER, ATTENTION OF THE COR.
6 ALL WALLS, INCLUDING FINISHES AND STRUCTURE, INDICATED BY DASHED LINES SHALL BE REMOVED.
7 AFTER REMOVAL OF EXISTING FLOOR, CONCRETE FLOOR SHALL BE GROUND SMOOTH BEFORE INSTALLATION OF NEW FINISH AT JUNCTIONS BETWEEN NEW AND EXISTING FLOORS, PROVIDE APPROPRIATE TRANSITION STRIP.
8 COORDINATE ABOVE CEILING WORK TO ENSURE ADEQUATE SPACE FOR INSTALLATION OF EACH TRADE ITEM AND TO ALLOW FOR SERVICE ACCESS FOLLOWING INSTALLATION. APPROPRIATE TRANSITION STRIP.

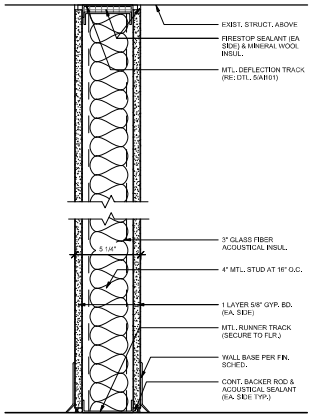

P1 SERIES PARTITION TYPE

P1	4" 20 GA. MTL STUDS NOT RATED W/ INSUL

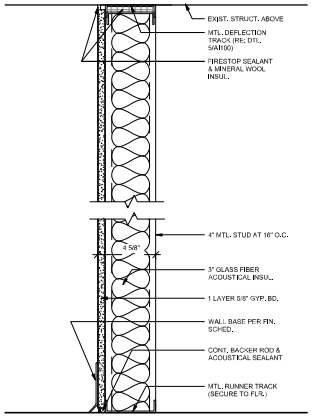

P2 SERIES PARTITION TYPE

P2	4" 20 GA. MTL STUDS NOT RATED W/ INSUL

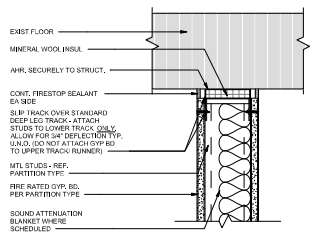

5 PARTITION TO STRUCTURE DETAIL

NO SCALE

NO	DESCRIPTION	DATE
0	100% SUBMITTAL	2/5/2025

ARCHITECTS/ENGINEERS:

9400 Ward Parkway
Kansas City, MO 64114
Phone: (816) 333-9400
Fax: (816) 822-3321
http://barnesmcd.com

Building Key Plan:

N

FACILITIES MANAGEMENT
FLOOR PLAN DRAWINGS

- FOR REFERENCE ONLY -
NOT FOR CONSTRUCTION

VA EASTERN KANSAS HEALTH CARE SYSTEM

Dwight D. Eisenhower VA Medical Center, Leavenworth
Colmery-O'Neil VA Medical Center, Topeka

Drawing Title:	**DEMOLITION / ARCHITECTUREAL PLAN**
Project Title:	**UPGRADE BUILDING 71 RESTROOMS FOR ADA COMPLIANCE**
Date:	2/5/26
Project No.	589A6-24-407
Scale:	AS NOTED
Building Number:	71
Checked By:	TJH
Drawn By:	PJR
Drawing No.	AI100
Approved:	
Location:	Dwight D. Eisenhower VA Medical Center, Leavenworth
Dwg.	Of

Department of Veterans Affairs

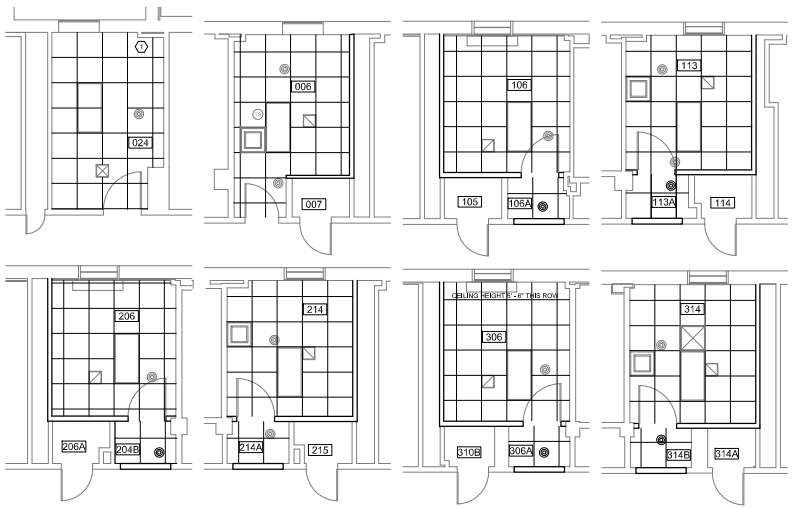

1 REFLECTIVE CEILING PLAN

1/4" = 1'-0"

KEYED INTERIOR DESIGN NOTES

1. THIS ROW OF CEILING TILES TO BE 7'-4".
2. REPLACE WALL MOUNTED COVER PLATES.
3. CENTER OPENING TO NEW RECESS. REFERENCE DET 3 / A102 FOR NEW TO EXISTING FLOOR TRANSITION.
4. REPLACE ACCESSORIES IN SIMILAR LOCATIONS AS EXISTING. ADA HEIGHTS MUST BE MET, SEE DET 6 / A102.
5. HEIGHT OF THREE CEILING TILES IN FRONT OF WINDOW TO BE DETERMINED BY DUCTWORK. COORDINATE WITH MECH CONTRACTOR.

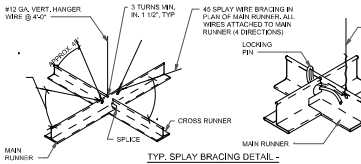

4 HUNG CEILING DETAIL

NO SCALE

LEGEND	
RECESSED LIGHT FIXTURE	WALL MOUNTED WATER CLOSET
WALL MOUNTED LIGHT FIXTURE	FLOOR MOUNTED WATER CLOSET
OCCUPANCY SENSOR	BIOHAZARDOUS DISPOSAL
SPRINKLER HEAD	AVIATORY
RETURN / EXHAUST GRILL / REGISTER	NEW TO EXISTING
SUPPLY DIFFUSER	SINGLE POLE SWITCH
2' x 2' ACOUSTICAL TILE CEILING	SANITARY NAPKIN DISPENSER
FIRE ALARM	

DEMOLITION GENERAL NOTES

1. REMOVE AND STORE ALL WALL MOUNTED RESTROOM ACCESSORIES INCLUDING ADA GRAB BARS, TOILET PAPER AND SOAP DISPENSERS, BIOHAZARD DISPOSAL, ETC. TO BE RE-USED.
2. DEMO ALL ARTIFICIAL MARBLE PARTITIONS AND WALL COVERINGS. WALL TILE AND WALL PLASTER TO CLAY TILE.
3. DEMO ALL FLOOR TILE AND TILE MORTAR TO STRUCTURE.
4. REPAIR ANY DAMAGE TO ITEM THAT ARE TO REMAIN.
5. DEMOLITION ITEMS MAY NOT BE ALL INCLUSIVE. REMOVE ALL ITEMS REQUIRED FOR NEW CONSTRUCTION ACTIVITIES.
6. FIELD VERIFY EXTENT OF EXISTING CONDITIONS FOR DEMOLITION WITH THE CONSTRUCTION DOCUMENTS AND SCHEDULED CONSTRUCTION PRIOR TO DEMOLITION. DISCREPANCIES BETWEEN DESIGN AND EXISTING CONDITIONS SHALL BE BROUGHT TO THE ATTENTION OF THE COR.
7. ALL WALLS, INCLUDING FINISHES AND STRUCTURE, INDICATED BY DASHED LINES SHALL BE REMOVED.
8. AFTER REMOVAL OF EXISTING FLOOR, CONCRETE FLOOR SHALL BE GROUND SMOOTH BEFORE INSTALLATION OF NEW FINISH AT JUNCTIONS BETWEEN NEW AND EXISTING FLOORS, PROVIDE APPROPRIATE TRANSITION STRIP.
9. WHERE EXISTING DOORS, DOOR FRAMES, EQUIPMENT, PORTIONS OF WALLS ARE REQUIRED TO BE REMOVED FOR THE COMPLETION OF THE WORK, EXERCISE CAUTION TO AVOID DISRUPTING SURROUNDING MATERIALS.
9. MAINTAIN CLEAR EXIT PATHS DURING DEMOLITION AND CONSTRUCTION.
10. ANY ASBESTOS FOUND DURING DEMOLITION SHALL BE BROUGHT TO THE ATTENTION OF THE COR. CONTRACTOR SHALL ENCAPSULATE AND ABATE THE AFFECTED AREA PER THE DIRECTION OF A LICENSED PROFESSIONAL ENVIRONMENTAL CONTRACTOR.
11. ALL STRUCTURAL ELEMENTS SHALL BE PROTECTED DURING DEMOLITION.
12. ASBESTOS REPORT INCLUDED WITH SPECIFICATIONS. CONTRACTOR TO NOTIFY COR UPON EXPOSURE OF INSULATED PLUMBING. ASBESTOS TESTING WILL BE PERFORMED BY VA.

GENERAL NOTES

1. ALL INFECTION CONTROL CRITERIA AS SPECIFIED IN THE SECTION 01 35 26 SHALL BE ADHERED TO DURING ALL PHASES OF THE PROJECT.
2. EXCEPT FOR ADA DIMENSIONS, ALL DIMENSIONS ARE APPROXIMATE SIZES. ALL CONSTRUCTION DIMENSIONS SHALL BE FIELD VERIFIED BY CONTRACTOR PRIOR TO THE START OF CONSTRUCTION.
3. COORDINATE MOUNTING LOCATIONS OF ALL WALL MOUNTED DEVICES AND/OR EQUIPMENT IN ORDER TO ELIMINATE CONFLICTS.
4. CONTRACTOR SHALL PROVIDE AND INSTALL ALL NECESSARY BLOCKING/ANCHORAGE FOR ALL WALL MOUNTED EQUIPMENT AND ACCESSORIES.
5. ALL ALARMS WILL BE KEPT CONNECTED AND IN WORKING ORDER, ATTENTION OF THE COR.
6. ALL WALLS, INCLUDING FINISHES AND STRUCTURE, INDICATED BY DASHED LINES SHALL BE REMOVED.
7. AFTER REMOVAL OF EXISTING FLOOR, CONCRETE FLOOR SHALL BE GROUND SMOOTH BEFORE INSTALLATION OF NEW FINISH AT JUNCTIONS BETWEEN NEW AND EXISTING FLOORS, PROVIDE APPROPRIATE TRANSITION STRIP.
8. COORDINATE ABOVE CEILING WORK TO ENSURE ADEQUATE SPACE FOR INSTALLATION OF EACH TRADE ITEM AND TO ALLOW FOR SERVICE ACCESS FOLLOWING INSTALLATION. APPROPRIATE TRANSITION STRIP.

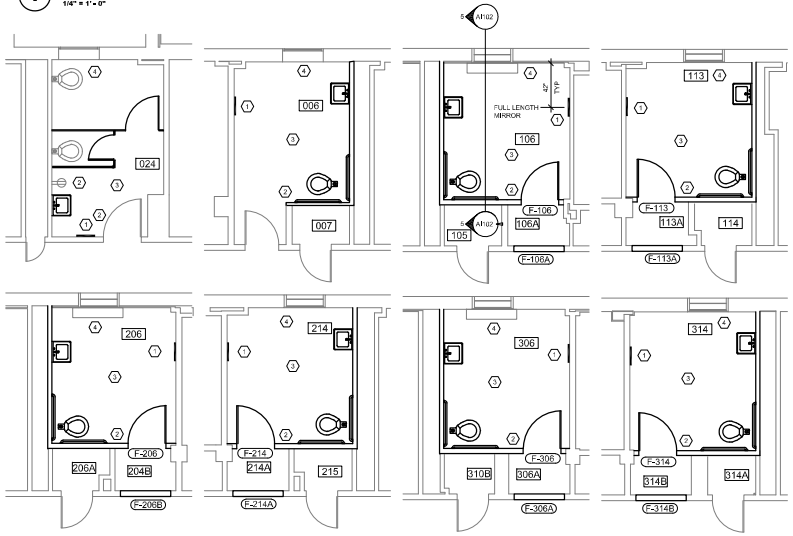

2 INTERIOR DESIGN PLAN

1/4" = 1'-0"

KEYED INTERIOR DESIGN NOTES

1. INSTALL FULL LENGTH MIRROR, SEE DET 6 FOR MOUNTING HEIGHT.
2. REPLACE COVER PLATE WITH NEW SS COVER PLATE. NEW COVER PLATE TBD BY VA.
3. REPLACE ACCESSORIES IN SIMILAR LOCATIONS AS EXISTING. ADA HEIGHTS MUST BE MET, SEE DET 6 / A102.
4. WINDOW TO BE SEALED AND RE-PAINTED. COLOR TBD BY VA.

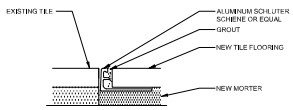

3 FLOOR TRANSITION DETAIL

NO SCALE

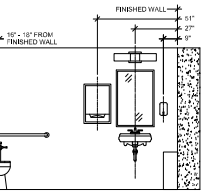

5 FIXTURE & ACCESSORIES ELEVATIONS

SCALE: ½" = 1'- 0"
AS SHOWN: RMS 106, 206, 306
MIRROR AS SHOWN: RMS 113, 214, 314

ROOM FINISH SCHEDULE

NUMBER	NAME	FLOOR	BASE	WALL	CEILING	COMMENTS
006	ACCESSIBLE TOILET	T-1	TB-1	T-1, T-2, TB-2 / EPW-1	ACT 9' - 0" AFF	DEVIATE AS SHOWN ON PLAN
024	TOILET	T-1	TB-1	T-1, T-2, TB-2 / EPW-1	ACT 7' - 11" AFF	
106	ACCESSIBLE TOILET	T-1	TB-1	T-1, T-2, TB-2 / EPW-1	ACT 7' - 6" AFF	
106A	RECESS	T-1	RB-1	P-1	ACT 7' - 6" AFF	
113	ACCESSIBLE TOILET	T-1	TB-1	T-1, T-2, TB-2 / EPW-1	ACT 8' - 1" AFF	
113A	RECESS	T-1	RB-1	P-1	ACT 8' - 1" AFF	
206	ACCESSIBLE TOILET	T-1	TB-1	T-1, T-2, TB-2 / EPW-1	ACT 7' - 4" AFF	
206A	RECESS	T-1	RB-1	P-1	ACT 7' - 4" AFF	
214	ACCESSIBLE TOILET	T-1	TB-1	T-1, T-2, TB-2 / EPW-1	ACT 7' - 6" AFF	
214A	RECESS	T-1	RB-1	P-1	ACT 7' - 6" AFF	
306	ACCESSIBLE TOILET	T-1	TB-1	T-1, T-2, TB-2 / EPW-1	ACT 8' - 0" AFF	
306A	RECESS	T-1	RB-1	P-1	ACT 8' - 0" AFF	DEVIATE AS SHOWN ON PLAN
314	ACCESSIBLE TOILET	T-1	TB-1	T-1, T-2, TB-2 / EPW-1	ACT 9' - 0" AFF	
314A	RECESS	T-1	RB-1	P-1	ACT 9' - 0" AFF	

TOILET AND HOUSEKEEPING CLOSET ACCESSORIES LEGEND EXISTING OR BY OWNER

MARK	ITEM	FURNISHED BY	DESCRIPTION
A1066	MIRROR, FLOAT GLASS, W/ SS FRAME	C / C	1/4" FLOAT GLASS, 36"H X 24"W, FRAMED
A1066	MIRROR, FLOAT GLASS, W/ SS FRAME	C / C	1/4" FLOAT GLASS, 60"H X 24"W, FRAMED
A5075	SOAP DISPENSER	V / C	SURFACED MOUNTED
A5080	PAPER TOWEL DISPENSER	V / C	SURFACED MOUNTED
A5090	SANITARY NAPKIN DISPOSAL	V / C	SURFACED MOUNTED
A5105	ADA GRAB BAR	C / C	42", MOUNTED PER ADA
A5200	TOILET TISSUE DISPENSER	V / C	TOILET TISSUE DISPENSER

NOTES:
1. PROVIDE NON-COMBUSTIBLE WOOD BLOCKING FOR ALL TOILET ACCESSORIES AS REQUIRED.
2. V/I = VA PROVIDED AND INSTALLED
   V/C = VA PROVIDED/CONTRACTOR INSTALLED
   C/C = CONTRACTOR PROVIDED AND INSTALLED

BASIS OF DESIGN COLOR SCHEDULE

T-1 DESC: FLOOR / WALL TILE
MANUF: CROSSVILLE / GOTHAM
COLOR: PRINTHOUSE AVIZO UPS
12" x 24" / T-1A GROUT

T-2 DESC: WALL TILE (ACCENT)
MANUF: CROSSVILLE / GOTHAM
COLOR: EBB & FLOW 8702
1/2" x 3" H MOSAIC / INSTALL VERTICALLY
3" H. SINGLE ROW / T-1A GROUT

TB-1 DESC: WALL TILE (BULLNOSE TRIM)
MANUF: CROSSVILLE / GOTHAM
COLOR: PRINTHOUSE AVIZO UPS
6" x 12" COVE BASE / T-1A GROUT

TB-2 DESC: WALL TILE (BULLNOSE TRIM)
MANUF: CROSSVILLE / GOTHAM
COLOR: PRINTHOUSE AVIZO UPS
4" x 24" BULLNOSE / T-1A GROUT

T-1A DESC: TILE GROUT
MANUF: TEC ACCUCOLOR
COLOR: LIGHT SMOKE
GROUT JOINT: 3/16" - 1/4"

EPW-1 DESC: EPOXY PAINT
MANUF: DURA-PLEX
COLOR: MATCH TO SHERWIN WILLIAMS BUNGALOW BEIGE 7511

P-1 DESC: WALL / TRIM
MANUF: SHERWIN WILLIAMS OR EQUAL
NO. SW 7069
COLOR: IRON ORE

RB-1 DESC: RESILIENT BASE
MANUF: RIDPRE / VINYL WALL BASE
COLOR: GINGERBREAD 677 / 6" H

ACT DESC: ACOUSTICAL TILE
MANUF: USG / RADAR / 2210 / SQUARE EDGE
SIZE: 2' x 2' / COLOR: WHITE
DOWN END DOUBLE RIVET / ACOUSTICAL SUSPENSION SYSTEM GRID / WHITE

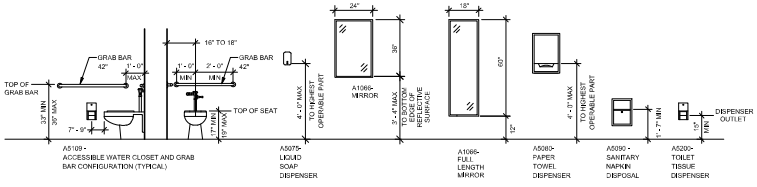

NOTE: MOUNTING HEIGHTS ARE TYPICAL UNLESS NOTED OTHERWISE.

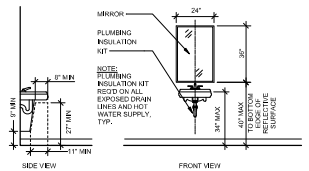

6 ELEVATION HEIGHTS

SCALE: ½" = 1'- 0"

NO	DESCRIPTION	DATE
0	100% SUBMITTAL	2/5/2026

ARCHITECTS/ENGINEERS:

9400 Ward Parkway
Kansas City, MO 64114
Phone: (816) 333-9400
Fax: (816) 822-3321
http://barnesmcd.com

Building Key Plan:

FACILITIES MANAGEMENT
FLOOR PLAN DRAWINGS

- FOR REFERENCE ONLY -
NOT FOR CONSTRUCTION

VA EASTERN KANSAS HEALTH CARE SYSTEM

Dwight D. Eisenhower VA Medical Center, Leavenworth
Colmery-O'Neil VA Medical Center, Topeka

Drawing Title: **REFLECTIVE CEILING / INTERIOR DESIGN PLAN**

Project Title: **UPGRADE BUILDING 71 RESTROOMS FOR ADA COMPLIANCE**

Date: 2/5/26

Project No. 589A6-24-407

Scale: AS NOTED

Approved:

Building Number: 71 | Checked By: TJH | Drawn By: PJR

Location: Dwight D. Eisenhower VA Medical Center, Leavenworth

Drawing No. AI101

Dwg. Of

Department of Veterans Affairs

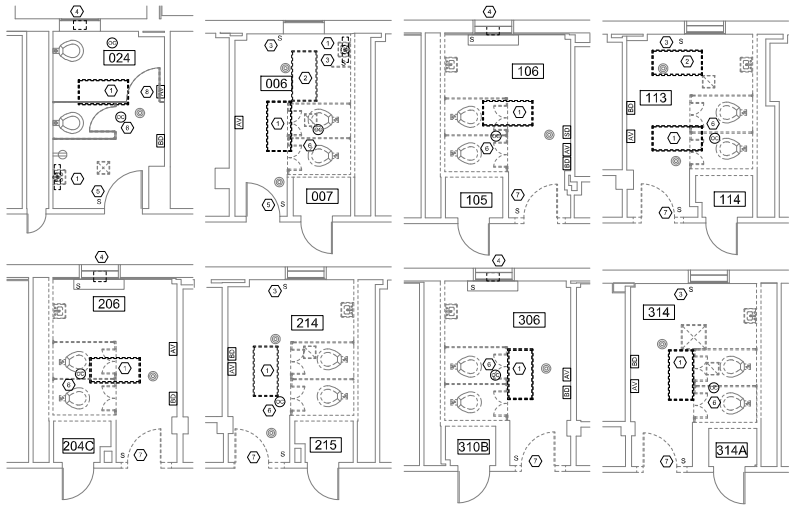

1 ELECTRICAL DEMOLITION PLAN

SCALE: 1/4" = 1'-0"

ELECTRICAL DEMO KEYED NOTES

1. DEMO LIGHT FIXTURE, CIRCUIT TO REMAIN FOR NEW FIXTURE. NEW FIXTURE MAY BE IN DIFFERENT LOCATION AND/OR ORIENTATION.
2. DEMO LIGHT FIXTURE. REMOVE UNUSED WIRING AND CONDUIT.
3. DEMO OUTLET / SWITCH. REMOVE UNUSED WIRING AND CONDUIT.
4. DEMO FAN AND ASSOCIATED SWITCH. CIRCUIT TO BE REUSED FOR NEW FAN LOCATED IN PLENUM. MECHANICAL CONTRACTOR TO DEMO FAN.
5. SWITCH AND COVER PLATE TO BE REPLACED.
6. OCCUPANCY SENSOR EXISTING TO REMAIN.
7. SWITCH AND COVER PLATE TO BE REPLACED AND RELOCATED. SWITCH TO REMAIN ON EXISTING CIRCUIT.
8. AIV FIRE ALARM SHALL ONLY BE MOVED AS NEEDED. KEEP ALARM CONNECTED TO POWER AT ALL TIMES. IF DISCONNECTED, CONTACT VA IMMEDIATELY AND PROVIDE FIRE WATCH.

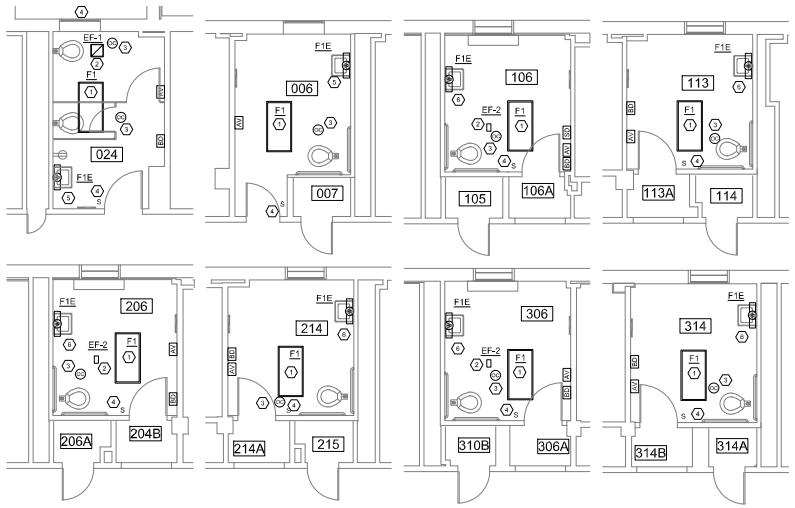

2 ELECTRICAL PLAN

SCALE: 1/4" = 1'-0"

ELECTRICAL DEMO KEYED NOTES

1. INSTALL NEW LIGHT FIXTURE, RE-USE EXISTING CIRCUIT.
2. POWER NEW EXHAUST FAN ABOVE CEILING USING EXISTING CIRCUIT.
3. OCCUPANCY SENSOR IS EXISTING TO REMAIN.
4. NEW SPST LIGHT SWITCH AND COVER PLATE TO BE REPLACED ON EXISTING LIGHT/FAN CIRCUIT. NEW COVER PLATE TBD BY VA.
5. INSTALL NEW LIGHT FIXTURE. BOTTOM OF LIGHT FIXTURE TO BE 6'-1" AFF. RE-USE EXISTING CIRCUIT.
6. INSTALL NEW LIGHT FIXTURE. POWER FROM EXISTING OVERHEAD LIGHT/FAN CIRCUIT. BOTTOM OF LIGHT FIXTURE TO BE 6'-6" AFF.

LEGEND

- RECESSED LIGHT FIXTURE
- WALL MOUNTED LIGHT FIXTURE
- OCCUPANCY SENSOR
- SPRINKLER HEAD
- RETURN / EXHAUST GRILL / REGISTER
- SUPPLY DIFFUSER
- 2' x 2' ACOUSTICAL TILE CEILING
- AIV FIRE ALARM
- WALL MOUNTED WATER CLOSET
- FLOOR MOUNTED WATER CLOSET
- BD BIOHAZARDOUS DISPOSAL
- LAVATORY
- NEW TO EXISTING
- S SINGLE POLE SWITCH
- SD SANITARY NAPKIN DISPENSER

DEMOLITION GENERAL NOTES

1. REMOVE AND STORE ALL WALL MOUNTED RESTROOM ACCESSORIES INCLUDING ADA GRAB BARS, TOILET PAPER AND SOAP DISPENSERS, BIOHAZARD DISPOSAL, ETC. TO BE RE-USED.
2. DEMO ALL ARTIFICIAL MARBLE PARTITIONS AND WALL COVERINGS. WALL TILE AND WALL PLASTER TO CLAY TILE.
3. DEMO ALL FLOOR TILE AND TILE MORTAR TO STRUCTURE.
4. REPAIR ANY DAMAGE TO ITEM THAT ARE TO REMAIN.
5. DEMOLITION ITEMS MAY NOT BE ALL INCLUSIVE. REMOVE ALL ITEMS REQUIRED FOR NEW CONSTRUCTION ACTIVITIES.
6. FIELD VERIFY EXTENT OF EXISTING CONDITIONS FOR DEMOLITION WITH THE CONSTRUCTION DOCUMENTS AND SCHEDULED CONSTRUCTION PRIOR TO DEMOLITION. DISCREPANCIES BETWEEN DESIGN AND EXISTING CONDITIONS SHALL BE BROUGHT TO THE ATTENTION OF THE COR.
6. ALL WALLS, INCLUDING FINISHES AND STRUCTURE, INDICATED BY DASHED LINES SHALL BE REMOVED.
7. AFTER REMOVAL OF EXISTING FLOOR, CONCRETE FLOOR SHALL BE GROUND SMOOTH BEFORE INSTALLATION OF NEW FINISH AT JUNCTIONS BETWEEN NEW AND EXISTING FLOORS, PROVIDE APPROPRIATE TRANSITION STRIP.
8. WHERE EXISTING DOORS, DOOR FRAMES, EQUIPMENT, PORTIONS OF WALLS ARE REQUIRED TO BE REMOVED FOR THE COMPLETION OF THE WORK, EXERCISE CAUTION TO AVOID DISRUPTING SURROUNDING MATERIALS.
9. MAINTAIN CLEAR EXIT PATHS DURING DEMOLITION AND CONSTRUCTION.
10. ANY ASBESTOS FOUND DURING DEMOLITION SHALL BE BROUGHT TO THE ATTENTION OF THE COR. CONTRACTOR SHALL ENCAPSULATE AND ABATE THE AFFECTED AREA PER THE DIRECTION OF A LICENSED PROFESSIONAL ENVIRONMENTAL CONTRACTOR.
11. ALL STRUCTURAL ELEMENTS SHALL BE PROTECTED DURING DEMOLITION.
12. ASBESTOS REPORT INCLUDED WITH SPECIFICATIONS. CONTRACTOR TO NOTIFY COR UPON EXPOSURE OF INSULATED PLUMBING. ASBESTOS TESTING WILL BE PERFORMED BY VA.

GENERAL NOTES

1. ALL INFECTION CONTROL CRITERIA AS SPECIFIED IN THE SECTION 01 35 26 SHALL BE ADHERED TO DURING ALL PHASES OF THE PROJECT.
2. EXCEPT FOR ADA DIMENSIONS, ALL DIMENSIONS ARE APPROXIMATE SIZES. ALL CONSTRUCTION DIMENSIONS SHALL BE FIELD VERIFIED BY CONTRACTOR PRIOR TO THE START OF CONSTRUCTION.
3. COORDINATE MOUNTING LOCATIONS OF ALL WALL MOUNTED DEVICES AND/OR EQUIPMENT IN ORDER TO ELIMINATE CONFLICTS.
4. CONTRACTOR SHALL PROVIDE AND INSTALL ALL NECESSARY BLOCKING/BACKING/BRACE FOR ALL WALL MOUNTED EQUIPMENT AND ACCESSORIES.
5. ALL ALARMS WILL BE KEPT CONNECTED AND IN WORKING ORDER, ATTENTION OF THE COR.
6. ALL WALLS, INCLUDING FINISHES AND STRUCTURE, INDICATED BY DASHED LINES SHALL BE REMOVED.
7. AFTER REMOVAL OF EXISTING FLOOR, CONCRETE FLOOR SHALL BE GROUND SMOOTH BEFORE INSTALLATION OF NEW FINISH AT JUNCTIONS BETWEEN NEW AND EXISTING FLOORS, PROVIDE APPROPRIATE TRANSITION STRIP.
8. COORDINATE ABOVE CEILING WORK TO ENSURE ADEQUATE SPACE FOR INSTALLATION OF EACH TRADE ITEM AND TO ALLOW FOR SERVICE ACCESS FOLLOWING INSTALLATION. APPROPRIATE TRANSITION STRIP.

LIGHTING SCHEDULE

ITEM	DESCRIPTION	L/L	MTG	DIMENSIONS L	W	H	DIA.	WATTS ANSI WATTS	PER	LED TYPE	QTY	ABSOLUTE LUMENS (MIN)	DRIVER VOLTS	TYPE	BASIS OF DESIGN
F1	2x4 VOLUMETRIC TROFFER WITH SMOOTH REFLECTOR.	O	RE	4'-0"	2'-0"	2 3/8"		37 W	FIX	LED	1	3800	120 V	0-10V	PHILIPS EVOKIT
F1E	SCONCE	O	RE	2'-3"	2"	4 3/4"		23.5 W	FIX	LED	2	3504	120 V	EM	OXYGEN LIGHTING VEGA BATHROOM SCONCE

NO	DESCRIPTION	DATE
0	100% SUBMITTAL	2/5/26

ARCHITECTS/ENGINEERS:

9400 Ward Parkway
Kansas City, MO 64114
Phone: (816) 333-9400
Fax: (816) 822-3321
http://barnesvoci.com

Building Key Plan:

N

FACILITIES MANAGEMENT
FLOOR PLAN DRAWINGS

- FOR REFERENCE ONLY -
NOT FOR CONSTRUCTION

VA EASTERN KANSAS HEALTH CARE SYSTEM

Dwight D. Eisenhower VA Medical Center, Leavenworth
Colmery-O'Neil VA Medical Center, Topeka

Drawing Title: **ELECTRICAL PLAN**

Project Title: **UPGRADE BUILDING 71 RESTROOMS FOR ADA COMPLIANCE**

Date: **2/5/26**

Project No. **589A6-24-407**

Scale: **AS NOTED**

Building Number: **71** | Checked By: **TJH** | Drawn By: **PJR**

Drawing No. **E100**

Approved:

Location: Dwight D. Eisenhower VA Medical Center, Leavenworth

Dwg. Of

Department of Veterans Affairs

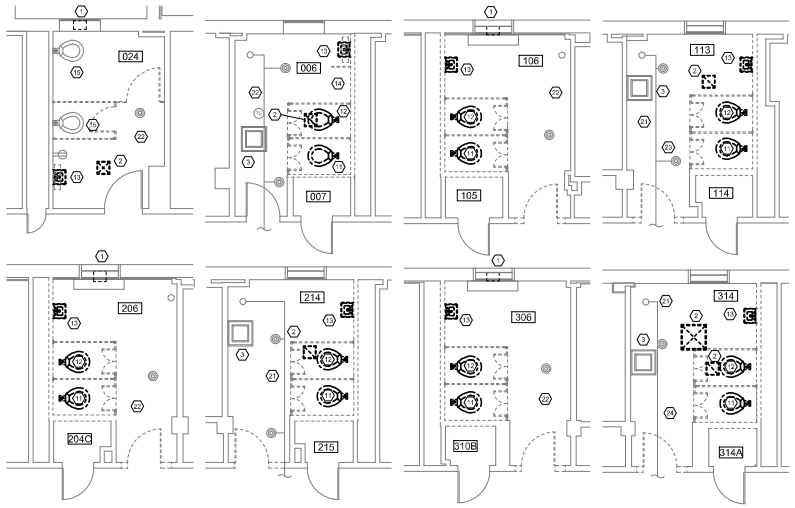

1 MECHANICAL / PLUMBING / FIRE PROTECTION DEMOLITION PLAN

SCALE: 1/4" = 1' - 0"

MECHANICAL DEMO KEYED NOTES

1 DEMO FAN MOUNTED IN WINDOW PANE. FAN MOUNTING PLATE AND GRAVITY DAMPER ARE EXISTING TO REMAIN.
2 DEMO DIFFUSER/GRILL. DUCTWORK TO REMAIN.
3 HVAC UNIT TO REMAIN. UNIT TO BE SUPPORTED WHILE CEILING GRID IS REPLACED.

PLUMBING DEMO KEYED NOTES

11 DEMO WC, WASTE, VENT AND CW TO BE RE-USED.
12 DEMO WC, WASTE AND VENT TO BE RE-USED. DEMO CW TO MAIN AND CAP.
13 DEMO LAV AND ASSOCIATED CARRIER. CW, HW, VENT AND WASTE TO BE USED.
14 DEMO URINAL AND ASSOCIATED CARRIER. DEMO WASTE, VENT AND CW TO MAIN AND CAP.
15 WATER CLOSET AND ASSOCIATED FLUSH VALVE AND CARRIER ARE EXISTING TO REMAIN. REMOVE DURING INTERIOR WORK.

FIRE PROTECTION DEMO KEYED NOTES

21 HORIZONTAL SPRINKLER PIPING LOCATED BELOW CEILING.
22 HORIZONTAL SPRINKLER PIPING LOCATED ABOVE CEILING.
23 SPRINKLER HEAD TO BE RELOCATED. CAP BRANCH AT MAIN.
24 SPRINKLER HEAD TO BE RELOCATED.

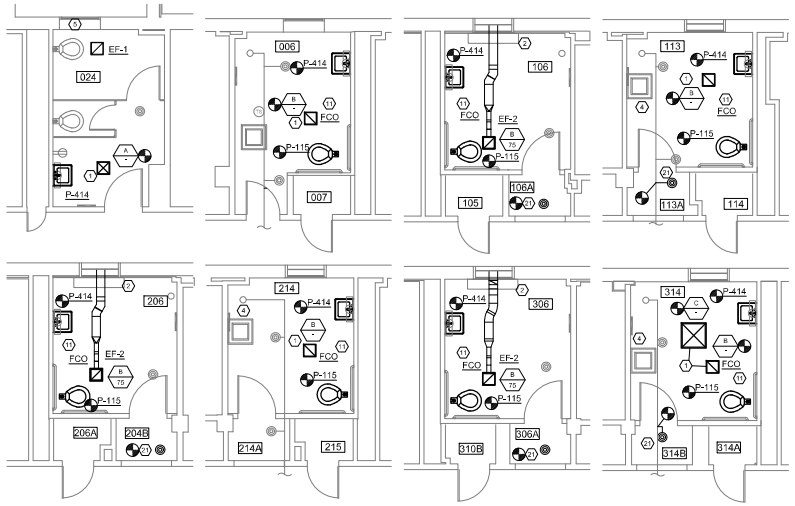

2 MECHANICAL / PLUMBING / FIRE PROTECTION PLAN

SCALE: 1/4" = 1' - 0"

MECHANICAL KEYED NOTES

1 INSTALL NEW DIFFUSER OR GRILL OF SIMILAR SIZE. DO NOT RE-BALANCE.
2 FLANGE TERMINAL END OF EXHAUST DUCT AND SECURE TO EXISTING FAN MOUNTING PLATE. USE SLIP FLANGE AND GASKETING. CONNECTION SHALL BE AIRTIGHT. MOUNT DUCTWORK AS HIGH AS POSSIBLE. COORDINATE CEILING HEIGHT WITH GEN CONTRACTOR.
3 RELOCATE THERMOSTAT 4' - 0" AFF.
4 REPLACE HVAC UNIT. AFTER INSTALLATION OF NEW CEILING GRID.
5 PROVIDE 8" DUCT FLANGE AND MOUNT TO EXISTING FAN MOUNTED PLATE. USE SLIP FLANGE AND GASKETING. CONNECTION SHALL BE TIGHT. PROVIDE 8' FLEX DUCT TO CONNECT TO EXHAUST FAN EF-1.

PLUMBING KEYED NOTES

11 INSTALL FLOOR CLEAN OUT AT DEMO'D WATER CLOSET WASTE CONNECTION.
12 INSTALL NEW WATER CLOSET. EXTEND EXISTING CW AND VENT LINES TO NEW WATER CLOSET.
13 INSTALL NEW LAVATORY AND ASSOCIATED CARRIER AND ADA INSULATION. EXTEND CW, HW AND VENT LINES TO NEW LAVATORY.
14 DEMO URINAL AND ASSOCIATED CARRIER. DEMO WASTE AND CW TO MAIN AND CAP AT MAIN.
15 REMOVE WATER CLOSET AND ASSOCIATED CARRIER. CAP WASTE AND CW. WATER CLOSET TO BE

FIRE PROTECTION KEYED NOTES

21 NEW SPRINKLER HEAD. ADD BRANCH LINE TO MAIN.

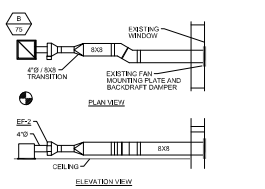

3 RM 106 AND 206 EXHAUST DETAIL

SCALE: 3/8" = 1' - 0"

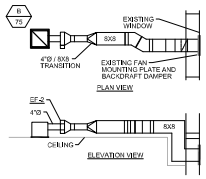

4 RM 306 EXHAUST DETAIL

SCALE: 3/8" = 1' - 0"

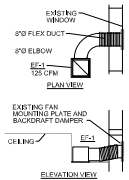

5 RM 024 EXHAUST DETAIL

SCALE: 3/8" = 1' - 0"

LEGEND

- RECESSED LIGHT FIXTURE
- WALL MOUNTED LIGHT FIXTURE
- OCCUPANCY SENSOR
- SPRINKLER HEAD
- RETURN / EXHAUST GRILL / REGISTER
- SUPPLY DIFFUSER
- 2' x 2' ACOUSTICAL TILE CEILING
- FIRE ALARM
- WALL MOUNTED WATER CLOSET
- FLOOR MOUNTED WATER CLOSET
- BIOHAZARDOUS DISPOSAL
- LAVATORY
- NEW TO EXISTING
- SINGLE POLE SWITCH
- SANITARY NAPKIN DISPENSER

DEMOLITION GENERAL NOTES

1 REMOVE AND STORE ALL WALL MOUNTED RESTROOM ACCESSORIES INCLUDING ADA GRAB BARS, TOILET PAPER AND SOAP DISPENSERS, BIOHAZARD DISPOSAL, ETC, TO BE RE-USED.
2 DEMO ALL ARTIFICIAL MARBLE PARTITIONS AND WALL COVERINGS. WALL TILE AND WALL PLASTER TO CLAY TILE.
3 DEMO ALL FLOOR TILE AND TILE MORTAR TO STRUCTURE.
4 REPAIR ANY DAMAGE TO ITEM THAT ARE TO REMAIN.
5 DEMOLITION ITEMS MAY NOT BE ALL INCLUSIVE. REMOVE ALL ITEMS REQUIRED FOR NEW CONSTRUCTION ACTIVITIES.
6 FIELD VERIFY EXTENT OF EXISTING CONDITIONS FOR DEMOLITION WITH THE CONSTRUCTION DOCUMENTS AND SCHEDULED CONSTRUCTION PRIOR TO DEMOLITION. DISCREPANCIES BETWEEN DESIGN AND EXISTING CONDITIONS SHALL BE BROUGHT TO THE ATTENTION OF THE COR.
6 ALL WALLS, INCLUDING FINISHES AND STRUCTURE, INDICATED BY DASHED LINES SHALL BE REMOVED.
7 AFTER REMOVAL OF EXISTING FLOOR, CONCRETE FLOOR SHALL BE GROUND SMOOTH BEFORE INSTALLATION OF NEW FINISH. AT JUNCTIONS BETWEEN NEW AND EXISTING FLOORS, PROVIDE APPROPRIATE TRANSITION STRIP.
8 WHERE EXISTING DOORS, DOOR FRAMES, EQUIPMENT, PORTIONS OF WALLS ARE REQUIRED TO BE REMOVED FOR THE COMPLETION OF THE WORK, EXERCISE CAUTION TO AVOID DISRUPTING SURROUNDING MATERIALS.
9 MAINTAIN CLEAR EXIT PATHS DURING DEMOLITION AND CONSTRUCTION.
10 ANY ASBESTOS FOUND DURING DEMOLITION SHALL BE BROUGHT TO THE ATTENTION OF THE COR. CONTRACTOR SHALL ENCAPSULATE AND ABATE THE AFFECTED AREA PER THE DIRECTION OF A LICENSED PROFESSIONAL ENVIRONMENTAL CONTRACTOR.
11 ALL STRUCTURAL ELEMENTS SHALL BE PROTECTED DURING DEMOLITION.
12 ASBESTOS REPORT INCLUDED WITH SPECIFICATIONS. CONTRACTOR TO NOTIFY COR UPON EXPOSURE OF INSULATED PLUMBING. ASBESTOS TESTING WILL BE PERFORMED BY VA.

GENERAL NOTES

1 ALL INFECTION CONTROL CRITERIA AS SPECIFIED IN THE SECTION 01 35 26 SHALL BE ADHERED TO DURING ALL PHASES OF THE PROJECT.
2 EXCEPT FOR ADA DIMENSIONS, ALL DIMENSIONS ARE APPROXIMATE SIZES. ALL CONSTRUCTION DIMENSIONS SHALL BE FIELD VERIFIED BY CONTRACTOR PRIOR TO THE START OF CONSTRUCTION.
3 COORDINATE MOUNTING LOCATIONS OF ALL WALL MOUNTED DEVICES AND/OR EQUIPMENT IN ORDER TO ELIMINATE CONFLICTS.
4 CONTRACTOR SHALL PROVIDE AND INSTALL ALL NECESSARY BLOCKING/ANCHORAGE FOR ALL WALL MOUNTED EQUIPMENT AND ACCESSORIES.
5 ALL ALARMS WILL BE KEPT CONNECTED AND IN WORKING ORDER, ATTENTION OF THE COR.
6 ALL WALLS, INCLUDING FINISHES AND STRUCTURE, INDICATED BY DASHED LINES SHALL BE REMOVED.
7 AFTER REMOVAL OF EXISTING FLOOR, CONCRETE FLOOR SHALL BE GROUND SMOOTH BEFORE INSTALLATION OF NEW FINISH. AT JUNCTIONS BETWEEN NEW AND EXISTING FLOORS, PROVIDE APPROPRIATE TRANSITION STRIP.
8 COORDINATE ABOVE CEILING WORK TO ENSURE ADEQUATE SPACE FOR INSTALLATION OF EACH TRADE ITEM AND TO ALLOW FOR SERVICE ACCESS FOLLOWING INSTALLATION. APPROPRIATE TRANSITION STRIP.

EXHAUST FAN SCHEDULE

MARK	DESCRIPTION	POWER	VOLT	RATED CFM	PRES. DROP	INLET SIZE	OUTLET SIZE	BASIS OF DESIGN
EF-1	CEILING MOUNTED VENTILATOR	27W MAX	120	138	0.1" H2O	10X10 INTEGRAL	8" DIA.	BROAN L100E
EF-2	INLINE CENTRIFUGAL FAN	20W MAX	120	135	0" H2O	4" DIA.	1.4" DIA.	FANTECH FG 4

NOTES: PROVIDE WITH MOUNTING BRACKET AND SPEED CONTROL

PLUMBING FIXTURE SCHEDULE

MARK	DESCRIPTION	DFU	CW WSFU	HW WSFU	TOTAL WSFU	WASTE PIPE SIZE INCHES	VENT PIPE SIZE INCHES	CW PIPE SUPPLY SIZE INCHES	HW PIPE SUPPLY SIZE INCHES
P-115	WATER CLOSET, FLUSH VALVE, PUBLIC, FLOOR MOUNTED	4	10	-	10	4	2	1	-
P-414	LAVATORY, PUBLIC	1	1.5	1.5	2.0	1.5	1.5	0.5	0.5
FCO	FLOOR CLEANOUT	-	-	-	-	EXISTING	N/A	N/A	-

AIR OUTLETS AND INLETS SCHEDULE

MARK	SERVICE	PD (IN W.C.)	FACE SIZE (IN)	MOUNT TYPE	NOISE CRITERIA	MATERIAL / COLOR
A	SUPPLY	0.1	12 X 12	LAY-IN	30	ALUMINUM / WHITE
B	EXHAUST	0.08	12 X 12	LAY-IN	30	ALUMINUM / WHITE
C	SUPPLY	0.1	24 X 24	LAY-IN	30	ALUMINUM / WHITE

NO	DESCRIPTION	DATE
0	100% SUBMITTAL	2/5/26

ARCHITECTS/ENGINEERS:

9400 Ward Parkway
Kansas City, MO 64114
Phone: (816) 333-9400
Fax: (816) 822-3321
http://barnesmcd.com

Building Key Plan:

N

FACILITIES MANAGEMENT
FLOOR PLAN DRAWINGS

- FOR REFERENCE ONLY -
NOT FOR CONSTRUCTION

VA EASTERN KANSAS HEALTH CARE SYSTEM

Dwight D. Eisenhower VA Medical Center, Leavenworth
Colmery-O'Neil VA Medical Center, Topeka

Drawing Title: **MECH / PLUMB / FIRE PROTECTION PLAN**

Project Title: **UPGRADE BUILDING 71 RESTROOMS FOR ADA COMPLIANCE**

Date: 2/5/26

Project No. 589A6-24-407

Scale: AS NOTED

Building Number: 71 | Checked By: TJH | Drawn By: PJR

Drawing No. MPF100

Dwg. Of

Approved:

Location: Dwight D. Eisenhower VA Medical Center, Leavenworth

Department of Veterans Affairs