



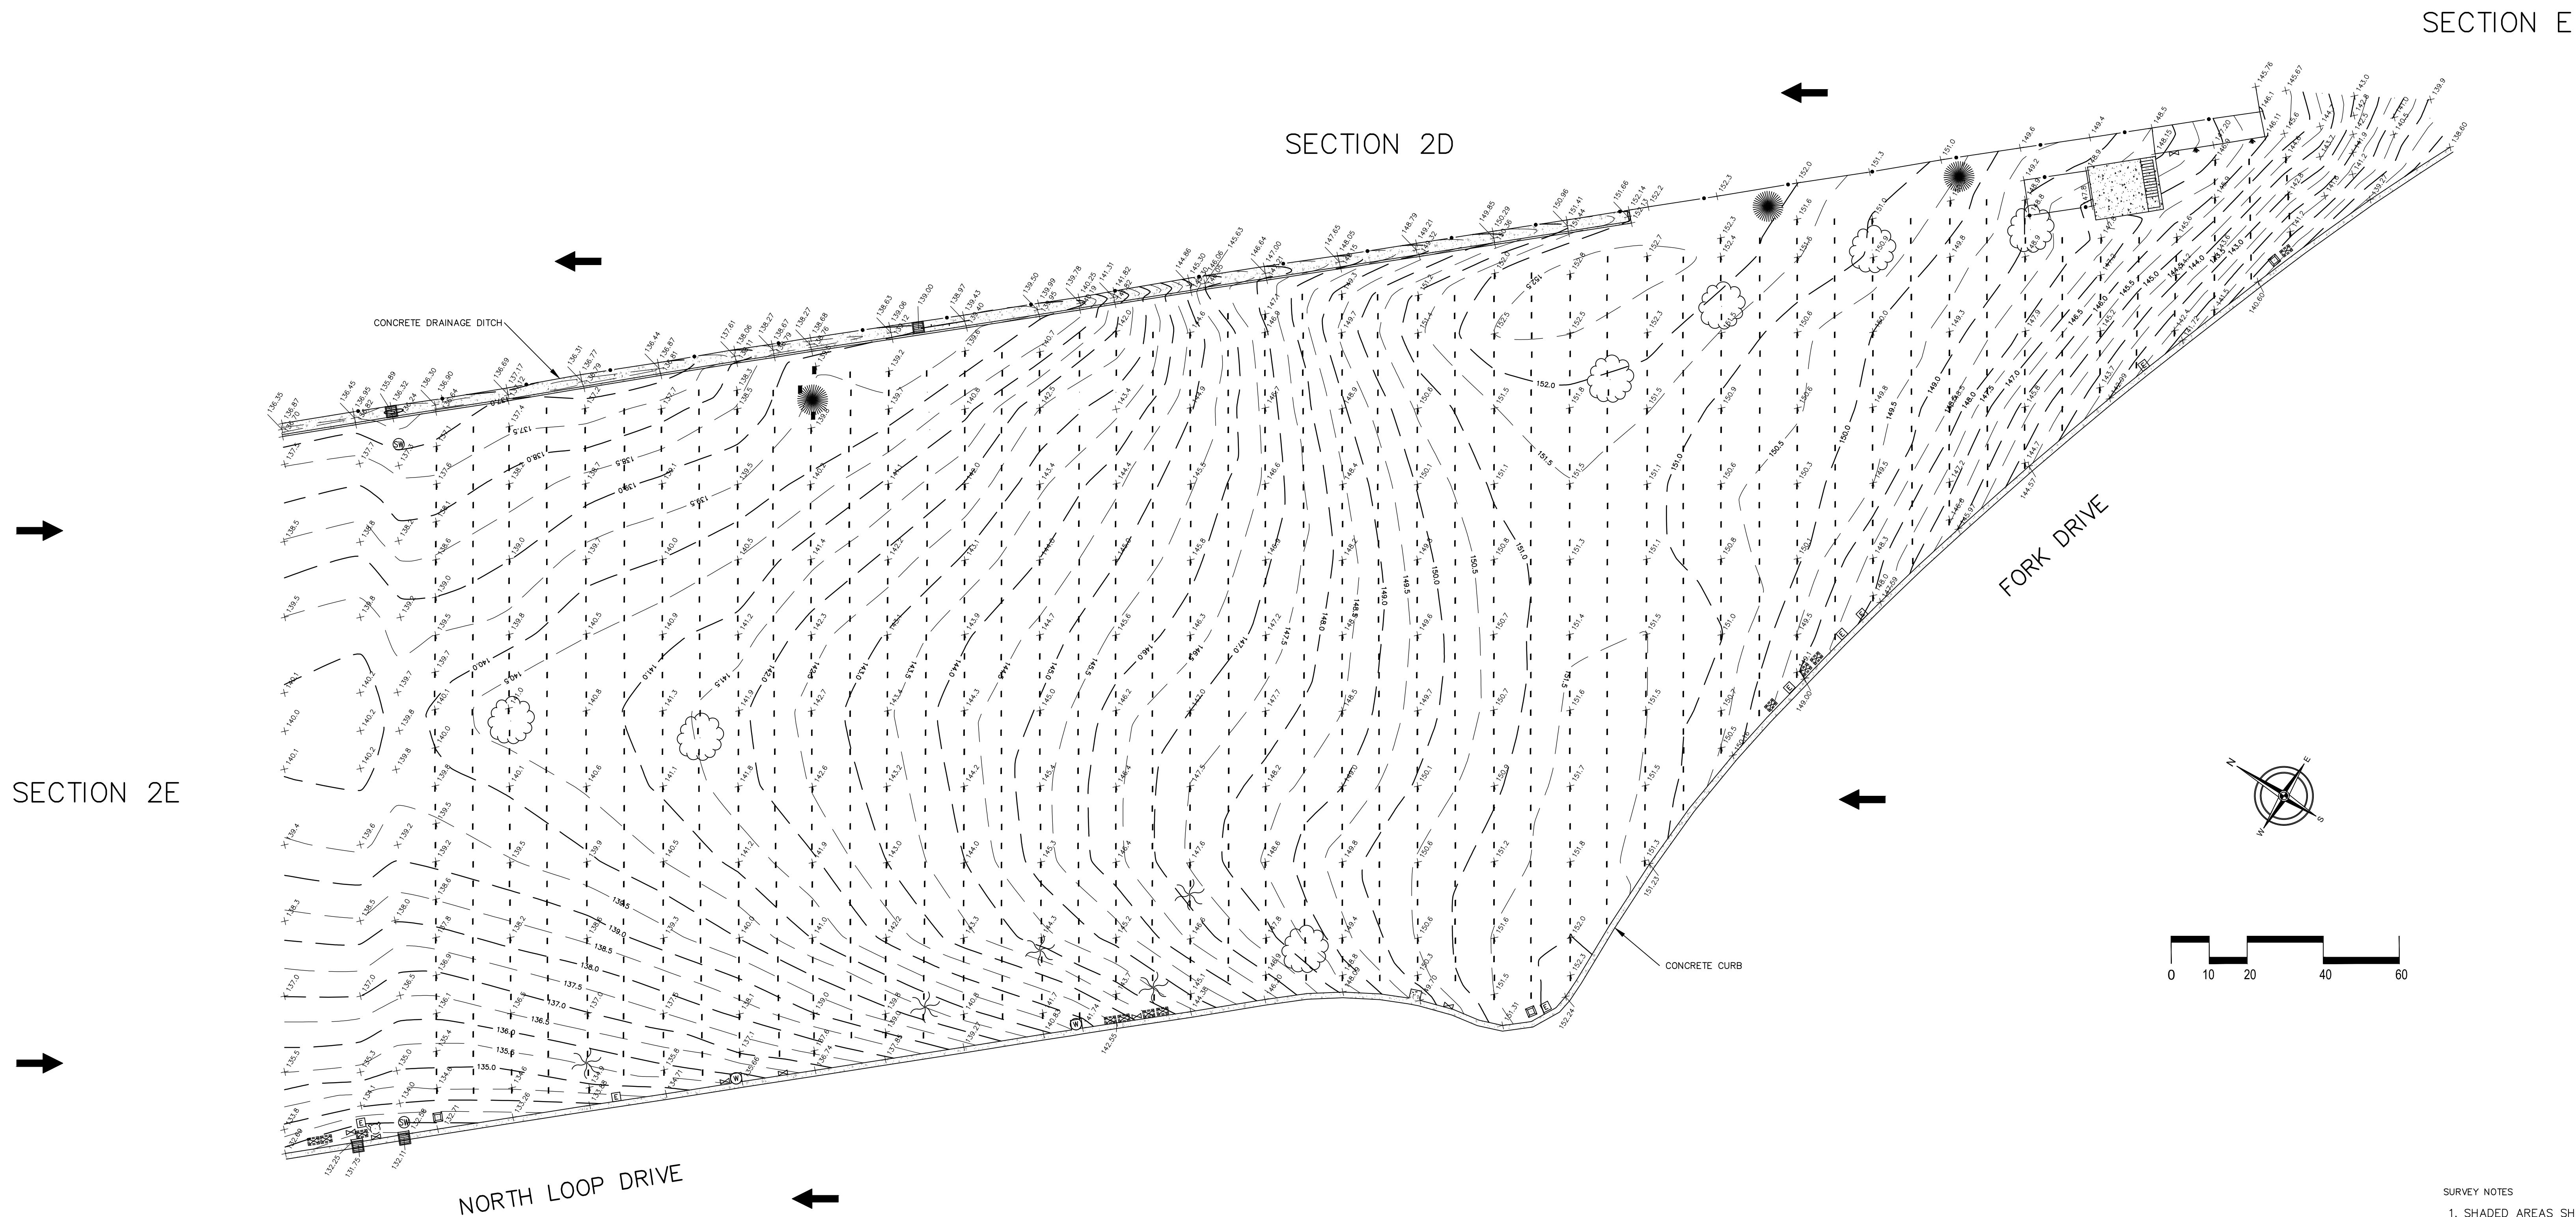

- GENERAL SYMBOLS
- EXISTING UPRIGHT HEADSTONE
 - EXISTING FLAT HEADSTONE
 - EXISTING UNKNOWN HEADSTONE
 - GRAVESITE CONTROL MONUMENT
 - CEMETERY SECTION MARKER
 - DIRECTION OF STONE FACE
 - SURVEY POINT SET (HUB & TACK)
 - ROAD SIGN
 - 1234 — NUMBER ON HEADSTONE
 - NO HEADSTONE
 - x 000.0 — EXISTING ELEVATION
 - 000.0 — PLAN ELEVATION
 - BROADLEAF TREE
 - EVERGREEN TREE
 - ORNAMENTAL TREE
 - PALM TREE
- LINE TYPES
- DESIGN HEADSTONE GRID
 - PROPOSED SOD LINE
 - CHAIN LINK FENCE
 - METAL PICKET FENCE
 - EXISTING CONTOUR
 - PLAN CONTOUR
- UTILITIES
- WATER SPIGOT
 - TRASH RECEPTACLE
 - ELECTRIC BOX
 - GATE VALVE
 - IRRIGATION VALVE BOX
 - IRRIGATION CONTROL PEDESTAL
 - FIRE HYDRANT
 - STORM DRAIN
 - STORM DRAINAGE INLET
 - STORM WATER MANHOLE
 - SANITARY SEWER MANHOLE


- SURVEY NOTES
1. SHADED AREAS SHOWN HEREON INDICATE HEADSTONES SHIFTING GREATER THAN 6".
 2. ELEVATIONS SHOWN HEREON ARE BASED UPON SAN BRUNO HVNC SB-3 AND HAVING AN ELEVATION OF 82.66' (NAVD 88).

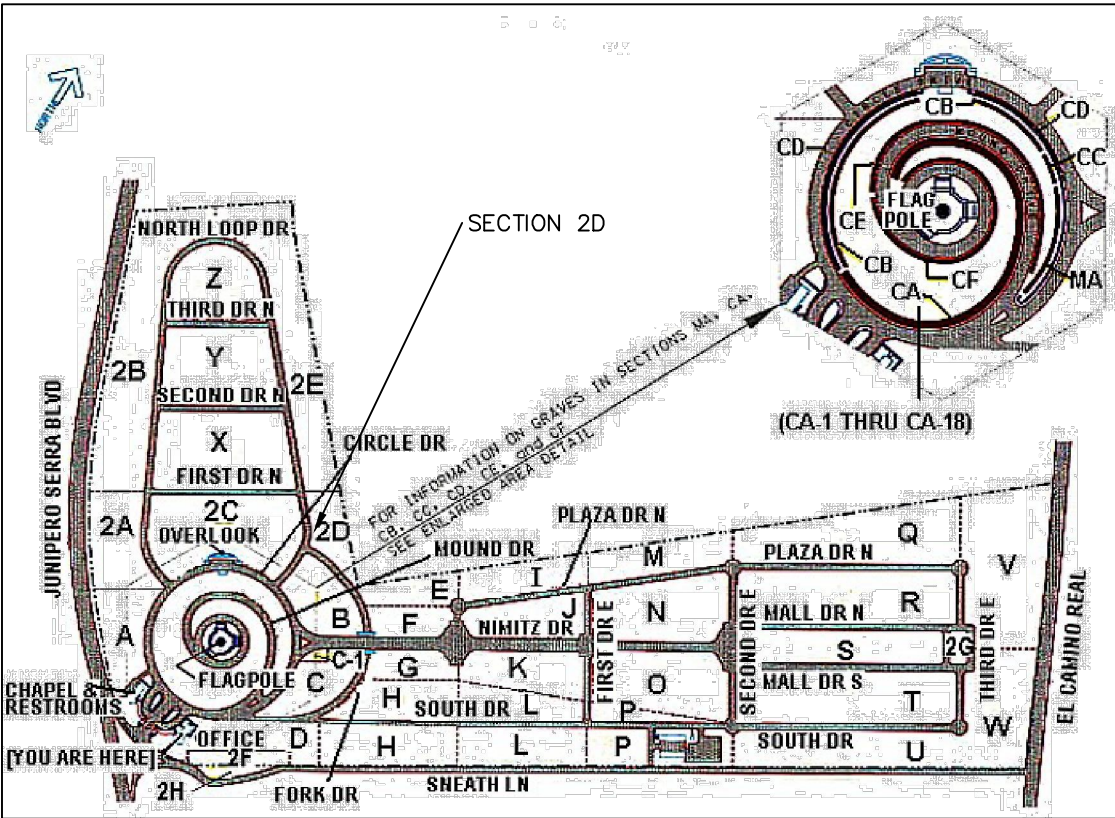

DATE OF FIELD SURVEY		CONSULTANTS	Exhibit 'E'	SECTION DATA								DRAWING TITLE		PROJECT TITLE		PROJECT NO.	
REVIEW COMMENTS – REVISED				SECTION	GRAVESITE GRID	HEADSTONES	NO. OF UPRIGHT	NO. OF FLAT	NO. OF RESERVED	AREA IN SQD	SECTION NO.						
				2D	5' X 10'	UPRIGHT MARBLE	1464	3			sqft			2D			
									</								

Exhibit 'E'

Example Site Survey, Headstone Realignment and Grading Plans

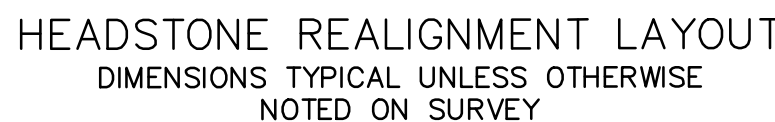

OFF-SET TO AVOID OBSTRUCTIONS. (TYPICAL)



1. SHADED AREAS SHOWN HEREON INDICATE HEADSTONES SHIFTING GREATER THAN 6".
2. ELEVATIONS SHOWN HEREON ARE BASED UPON SAN BRUNO HVCN SB-3 AND HAVING AN ELEVATION OF 82.66' (NAVD 88).

DATE OF FIELD SURVEY		CONSULTANTS	SECTION DATA							DRAWING TITLE HEADSTONE REALIGNMENT LAYOUT	PROJECT TITLE NATIONAL CEMETERY NATIONAL SHRINE PROJECT			PROJECT NO. N/A	
REVIEW COMMENTS – REVISED			SECTION	GRAVESITE GRID	HEADSTONES	NO. OF UPRIGHT	NO. OF FLAT	NO. OF RESERVED	AREA IN SOD		SECTION NO. 2D				
			2D	5' X 10'	UPRIGHT MARBLE	1464	3		sqft						
REVISIONS	DATE									APPROVED: CONTRACTING OFFICER REPRESENTATIVE	LOCATION			DRAWING NO. GGNC-2D DWG. 1 OF 2	
											DATE	DRAWN	CHECKED		

