


GENERAL SHEET NOTES

1. FOR GENERAL STRUCTURAL NOTES, LEGEND, AND STRUCTURAL TECHNICAL TERMS SEE DRAWING S-001.

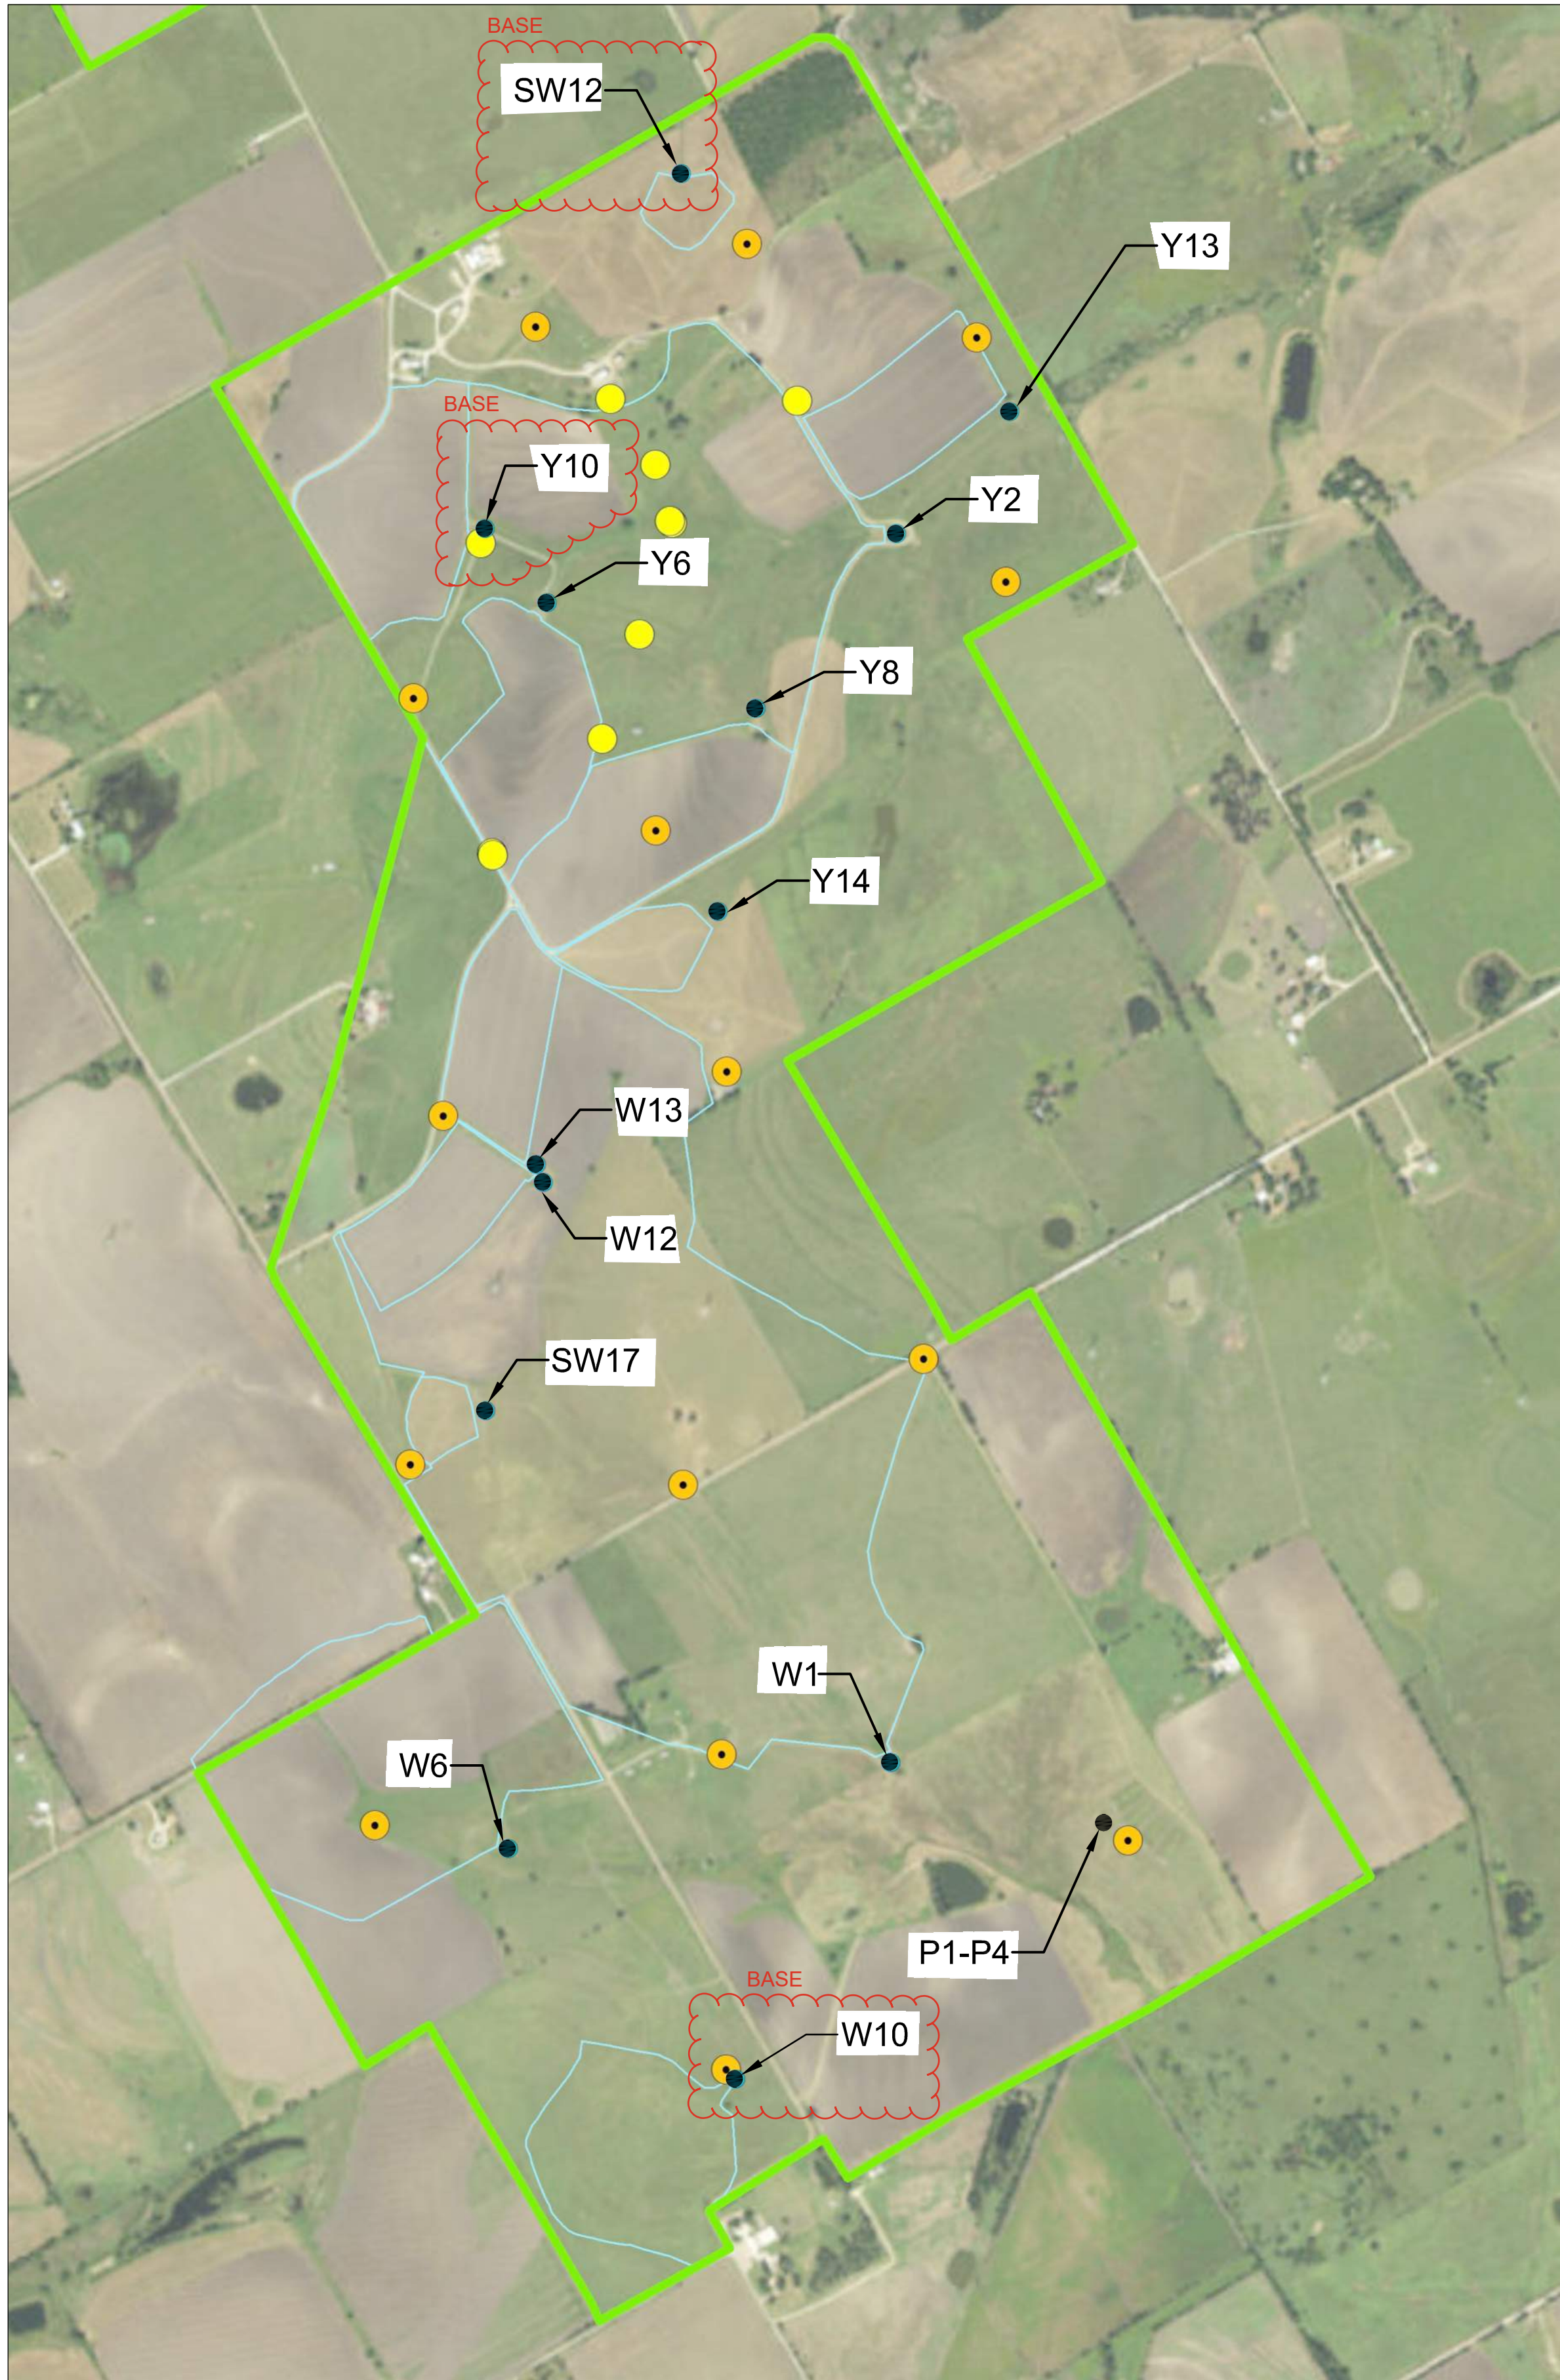

RUNOFF STATIONS LOCATION PLAN

SCALE: 1"=700'



STV Incorporated
255 West Vaden Drive
Douglasville, Pennsylvania
tel: 610-385-6000 fax: 610-385-6501
www.stvinc.com

A-E FIRM

USDA

PROJECT MANAGER

EFM

R. NEFF

N. GIRKEN

DESIGNER

LM

S. CHAMBERS

D. SMITH

CHECKED BY

SAFETY & HEALTH

M. HIGH

P. JOVANOVICH

DRAWN BY

REAL PROPERTY

W. HELLER

L. WURZBERGER

A	12/22/23	R. NEFF	ISSUED FOR BID
NO.	DATE	BY	DESCRIPTION
REVISIONS			
U S D A	 Agricultural Research Service		
	RUNOFF STATION - GRASSLAND, SOIL AND WATER RESEARCH LABORATORY (GSWRL) 1700 BLACKLAND ROAD, RIESEL, TEXAS 76869		
	RUNOFF STATIONS LOCATION PLAN		
	FACILITIES MODERNIZATION BRANCH (FMB) FACILITIES DIVISION (FD) 5901 SUNNYSIDE AVENUE SELTOVILLE, MO 65755		
SOLICITATION NO.			RIESEL S-003
DATE			DWG NO.



1/4"=1'-0"

0 2' 4' 8'



1. INSTALL POLYMER MODIFIED TOPPING SLAB.
2. RECONSTRUCT CONCRETE WALLS.
3. REINSTALL METAL ROOF. CONNECT TO CONCRETE WALLS TO MATCH EXISTING CONDITION.
4. #4@12 BY 30" LG EPOXY ANCHOR TO EXISTING WALLS (4" EMBED)

					
STV Incorporated 205 West Valley Drive Douglassville, Pennsylvania 19330 tel: 610-385-8200 fax: 610-385-8501 www.stvtv.com		A	12/22/23	R. NEFF	ISSUED FOR BID
		NO.	DATE	BY	DESCRIPTION
		REVISIONS			
		U S D A			
			Agricultural Research Service		
			RUNOFF STATION - GRASSLAND, SOIL AND WATER RESEARCH LABORATORY (GSWRL) 1702 BLACKLAND ROAD, REESEL, TEXAS 76662		
			RUNOFF STATION SW12 REPAIRS		
A-E FIRM		USDA			
PROJECT MANAGER	EPH				
R. NEFF	N. GIKEN				
DESIGNER	LM				
S. CHAMBERS	D. SMITH				
CHECKED BY	SAFETY & HEALTH				
S. CHAMBERS	P. JOVANOVIH				
DRAWN BY	REAL PROPERTY				
R. MARTIN	L. WURZBERGER				
		SOLICITATION NO.	FACILITIES MODERNIZATION BRANCH (FMB) FACILITIES DIVISION (FD) 5601 SUNSHINE DRIVE BELTSVILLE MD 20705		RIESEL SA-107
		DATE			(DAY) MO



GENERAL SHEET NOTES

- FOR GENERAL STRUCTURAL NOTES, LEGEND, AND STRUCTURAL TECHNICAL TERMS SEE DRAWING S-001.
- FOR RUNOFF STATION LOCATION PLAN SEE DRAWING S-003.
- CRACK WIDTH=1/16" UNO






SHEET KEYNOTES

- SAW CUT AND REMOVE CONCRETE OUTFALL RETAINING WALLS AS INDICATED ON PLAN IN THEIR ENTIRETY.
- REMOVE OUTFALL SLAB IN ITS ENTIRETY.
- REMOVE WOOD RETAINING WALL ON BOTH SIDES OF OUTFALL IN THEIR ENTIRETY.
- TEMPORARILY SUPPORT OR REMOVE METAL ROOF AND REINSTALL. MODIFY ROOF FRAMING TO FASTEN TO TOP OF NEW CONCRETE WALL.
- REMOVE 7" HIGH BY 5" THICK CONCRETE WALL.

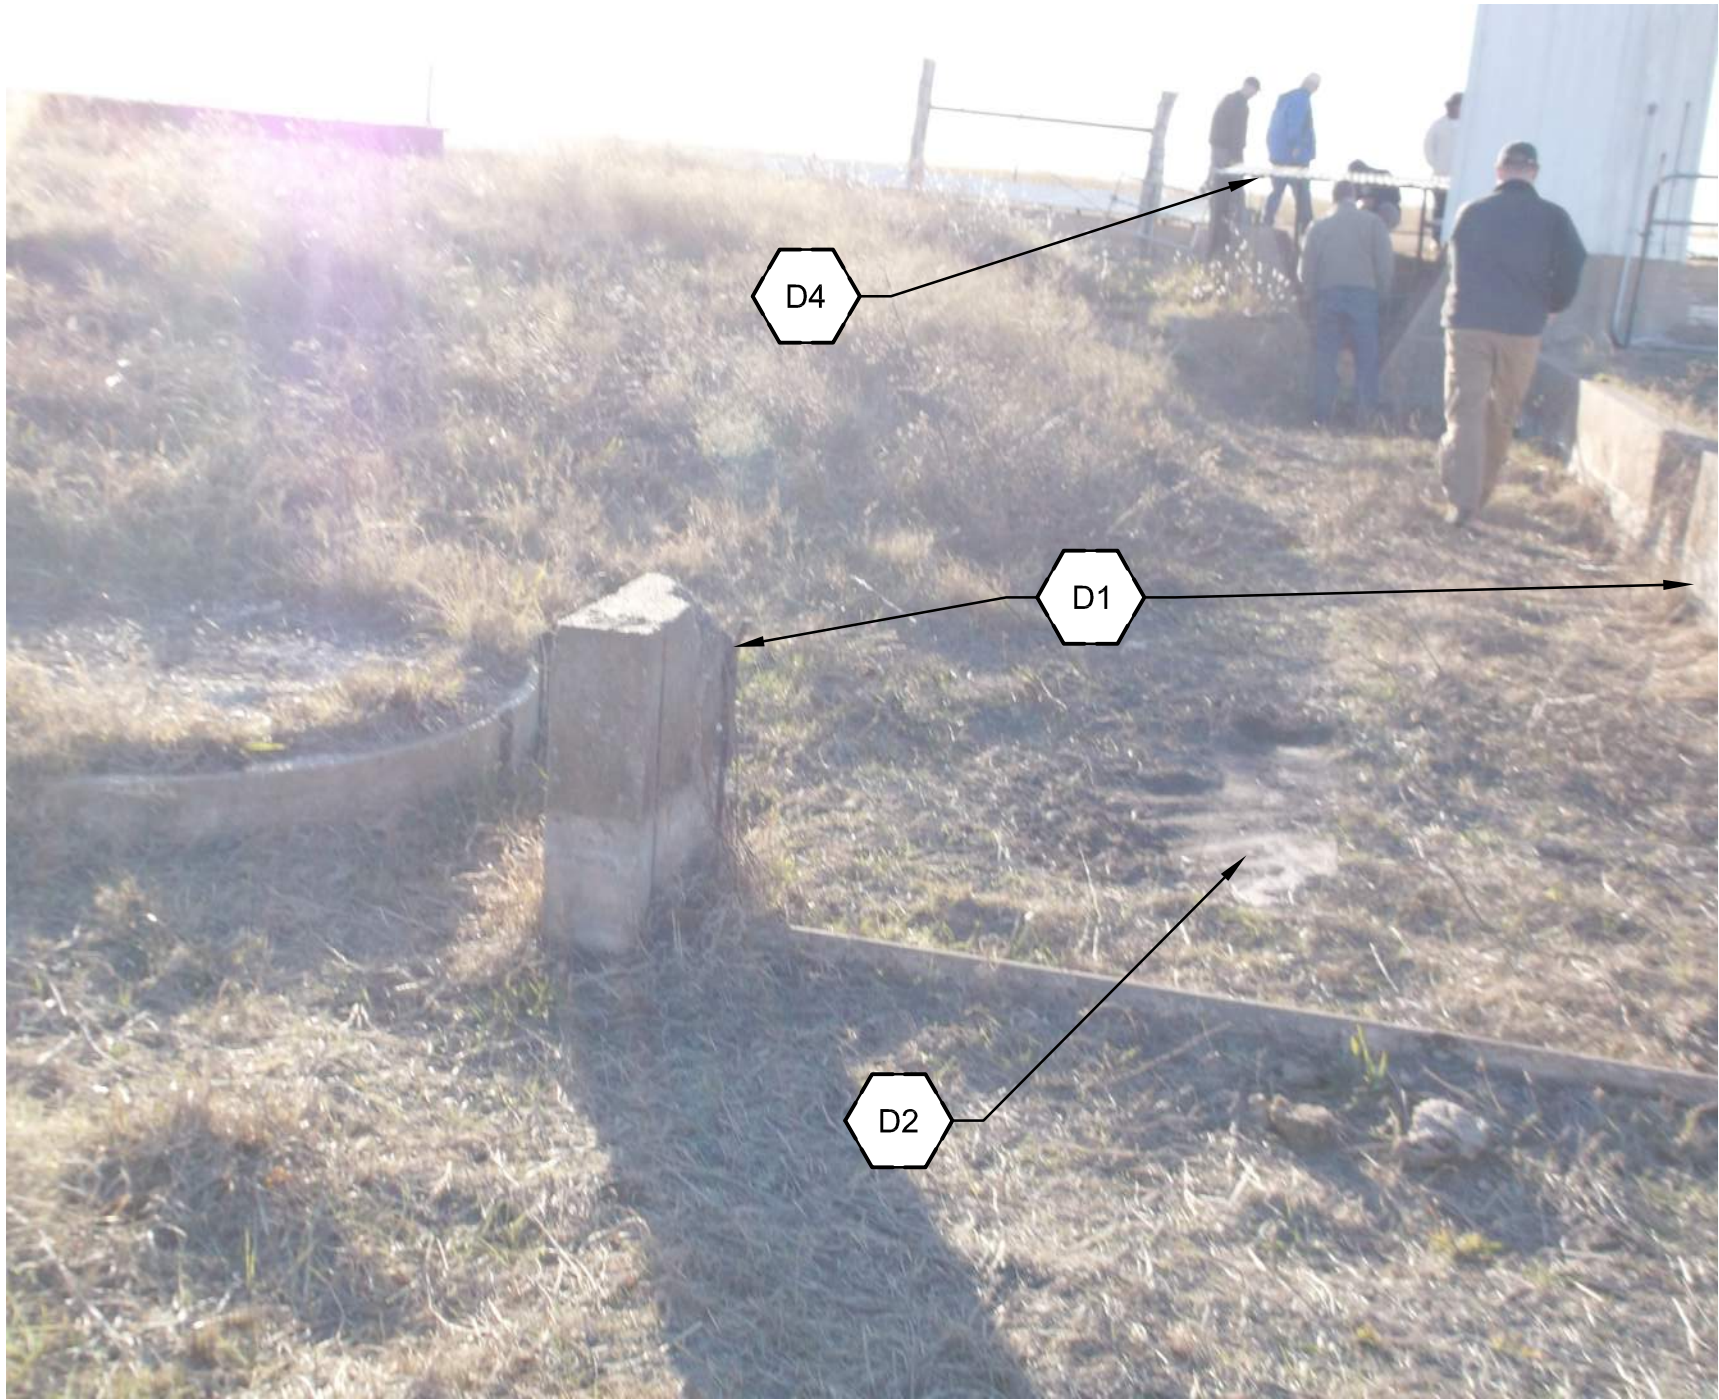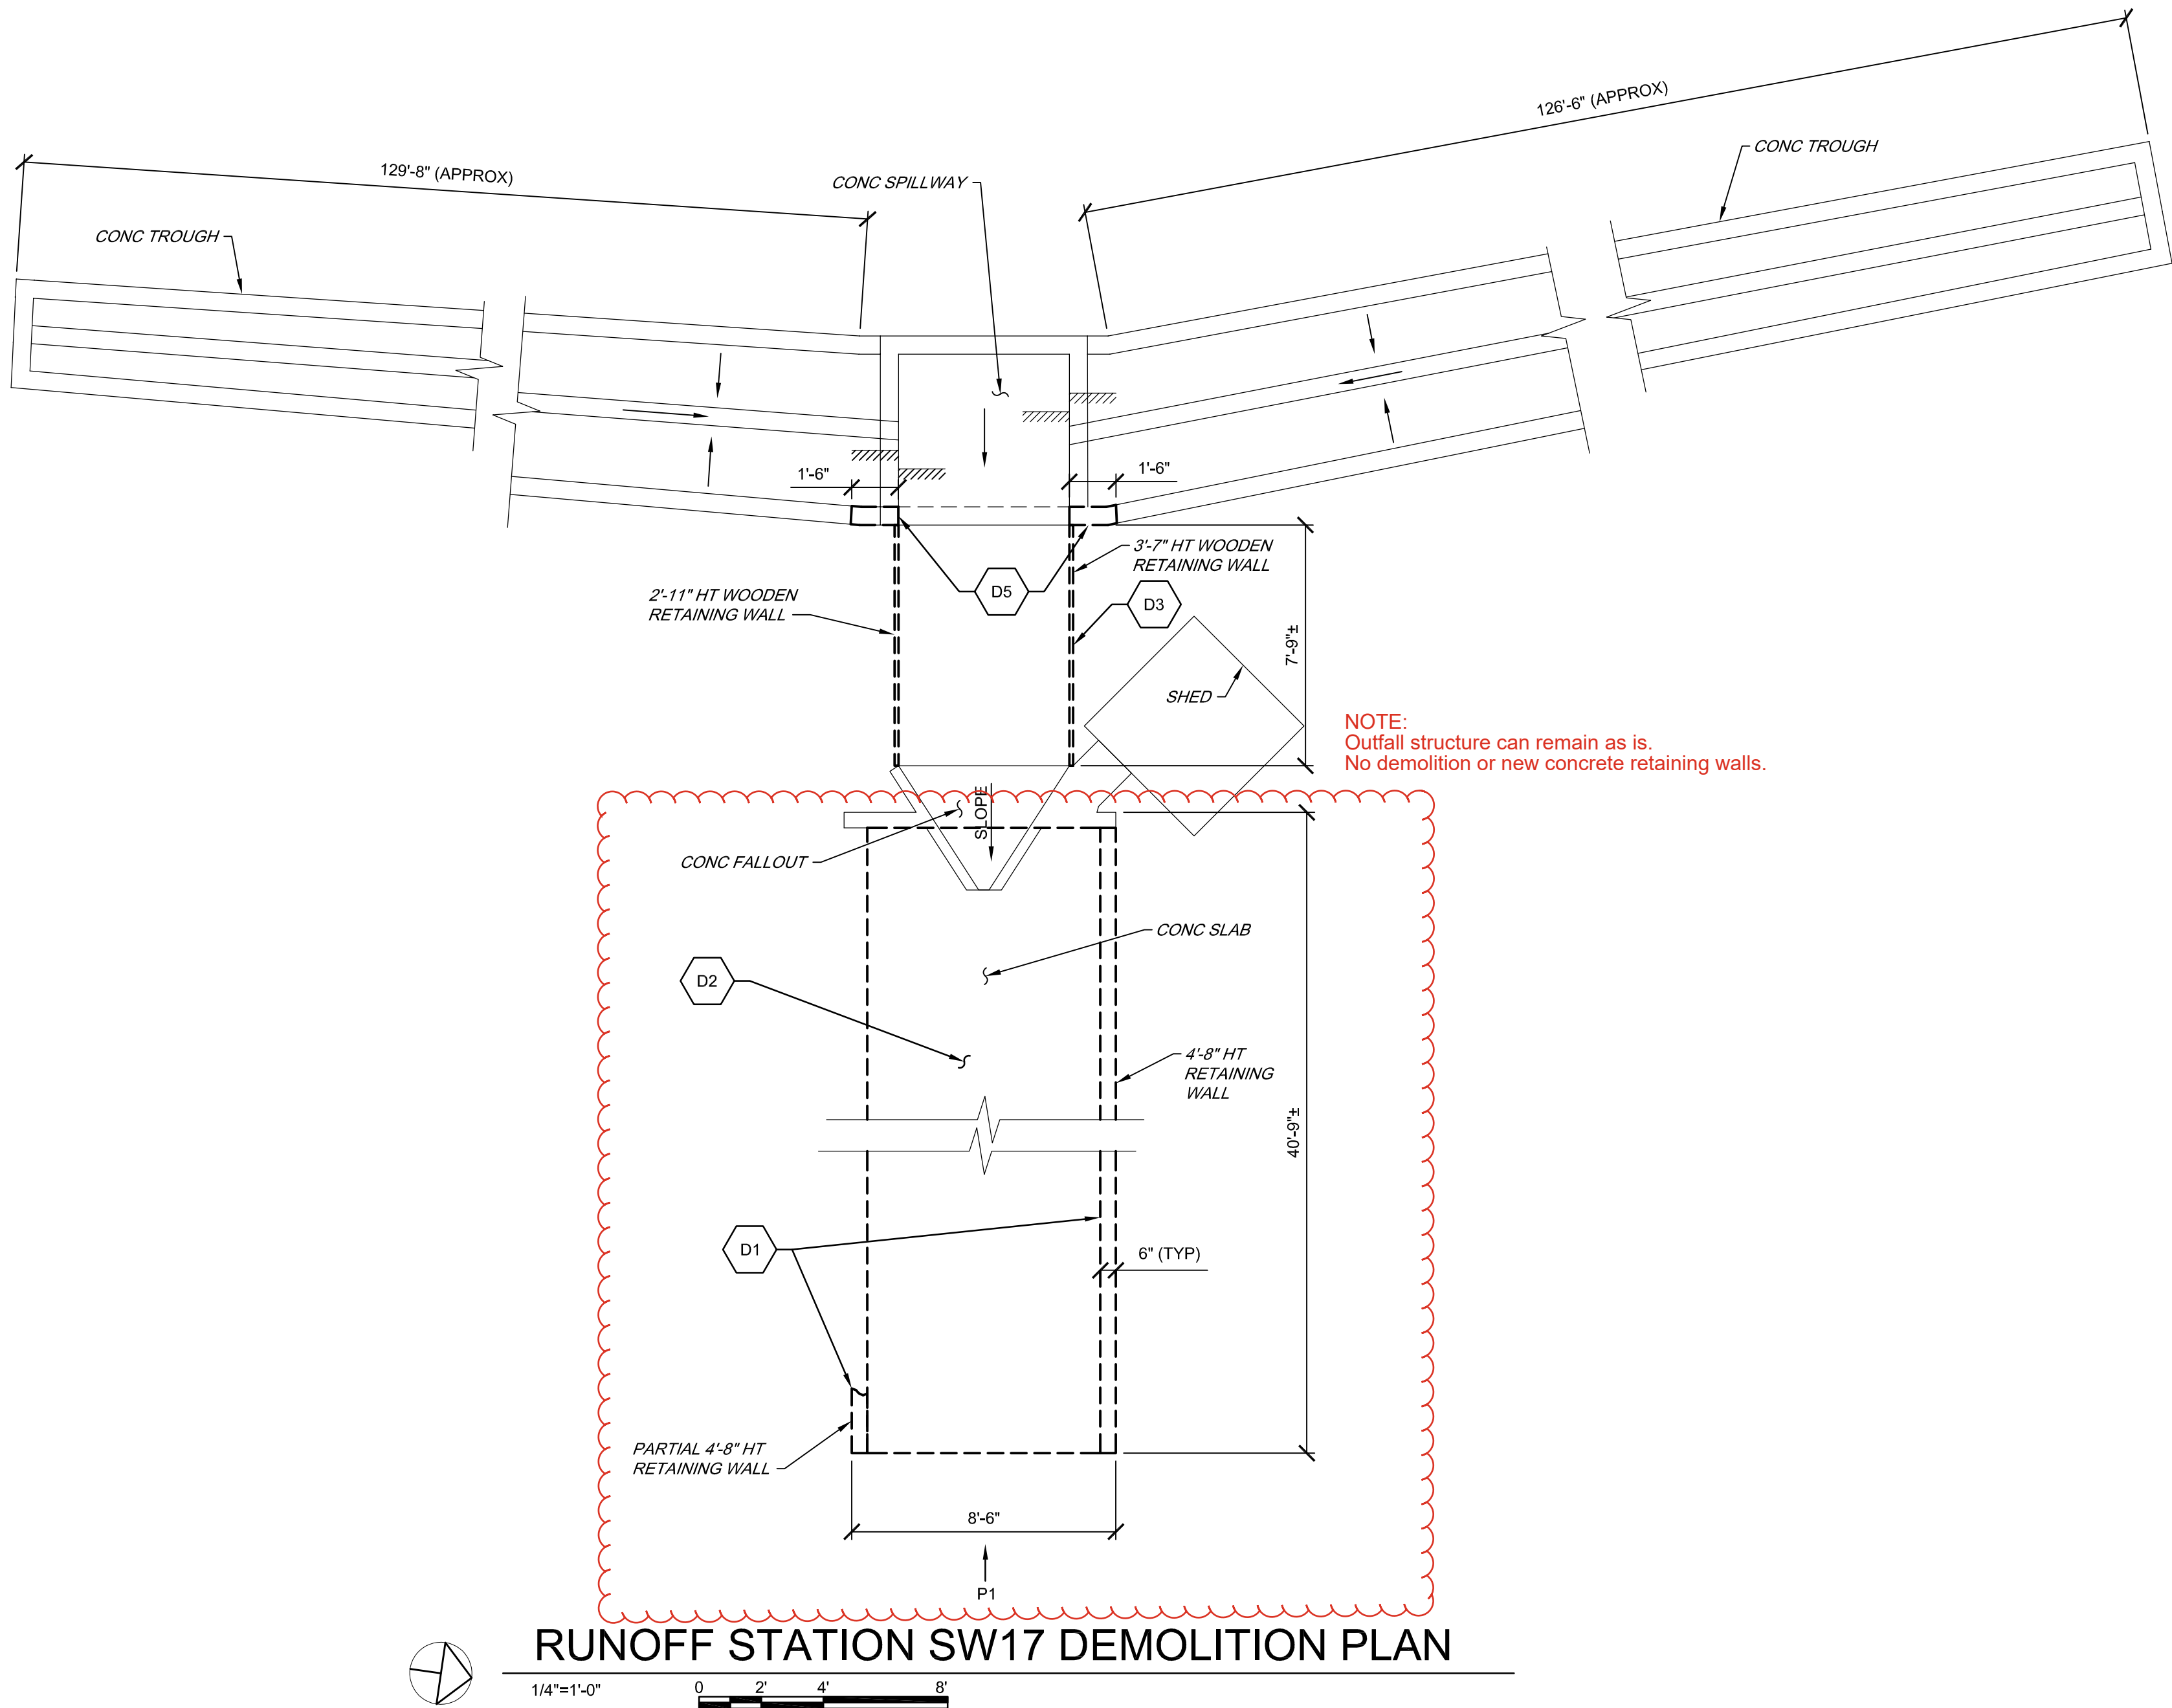

P1

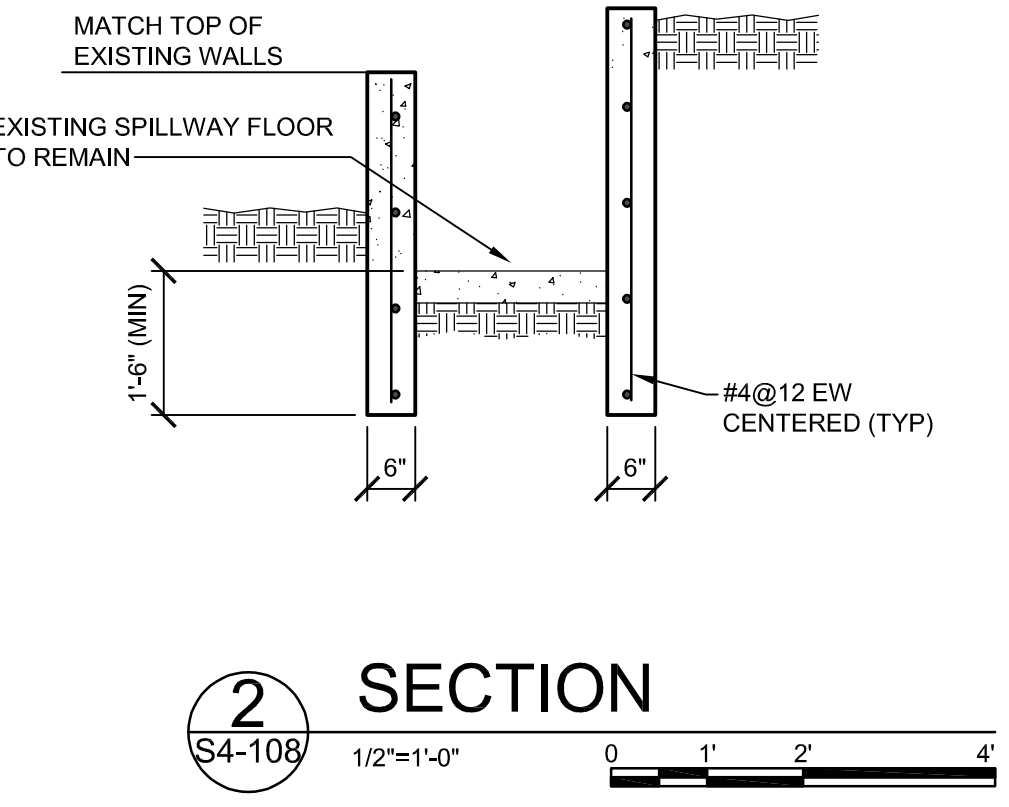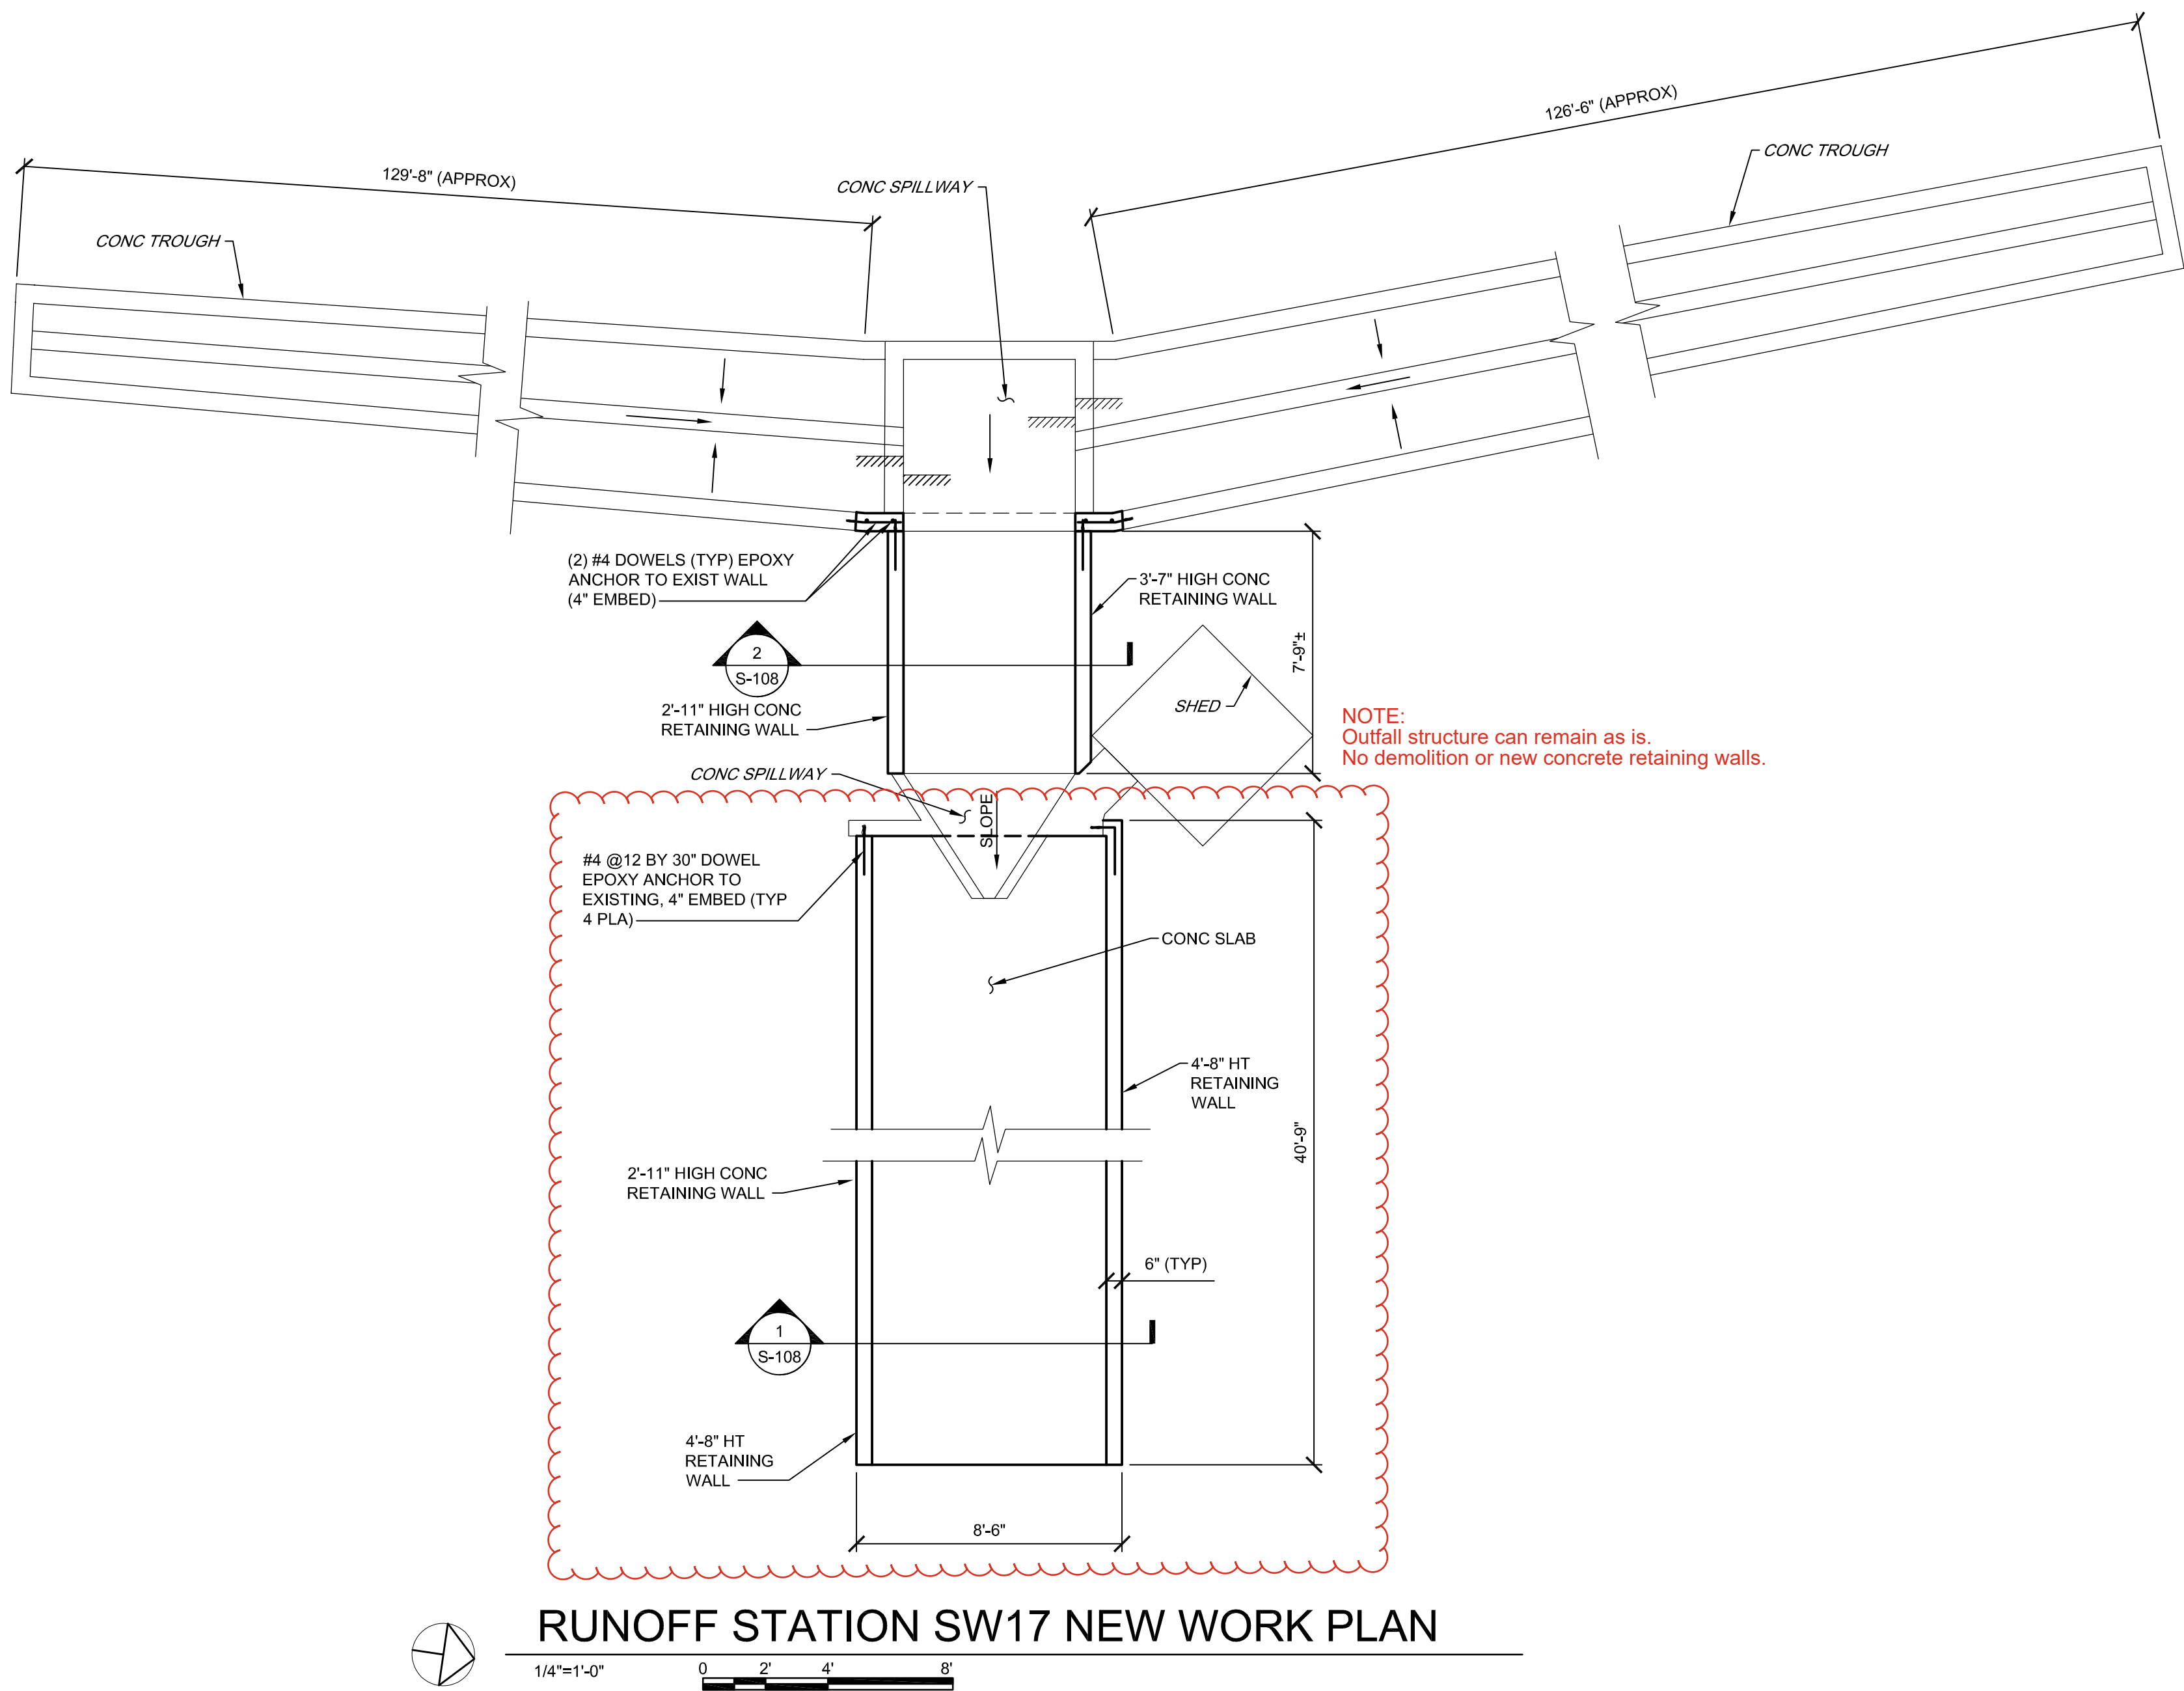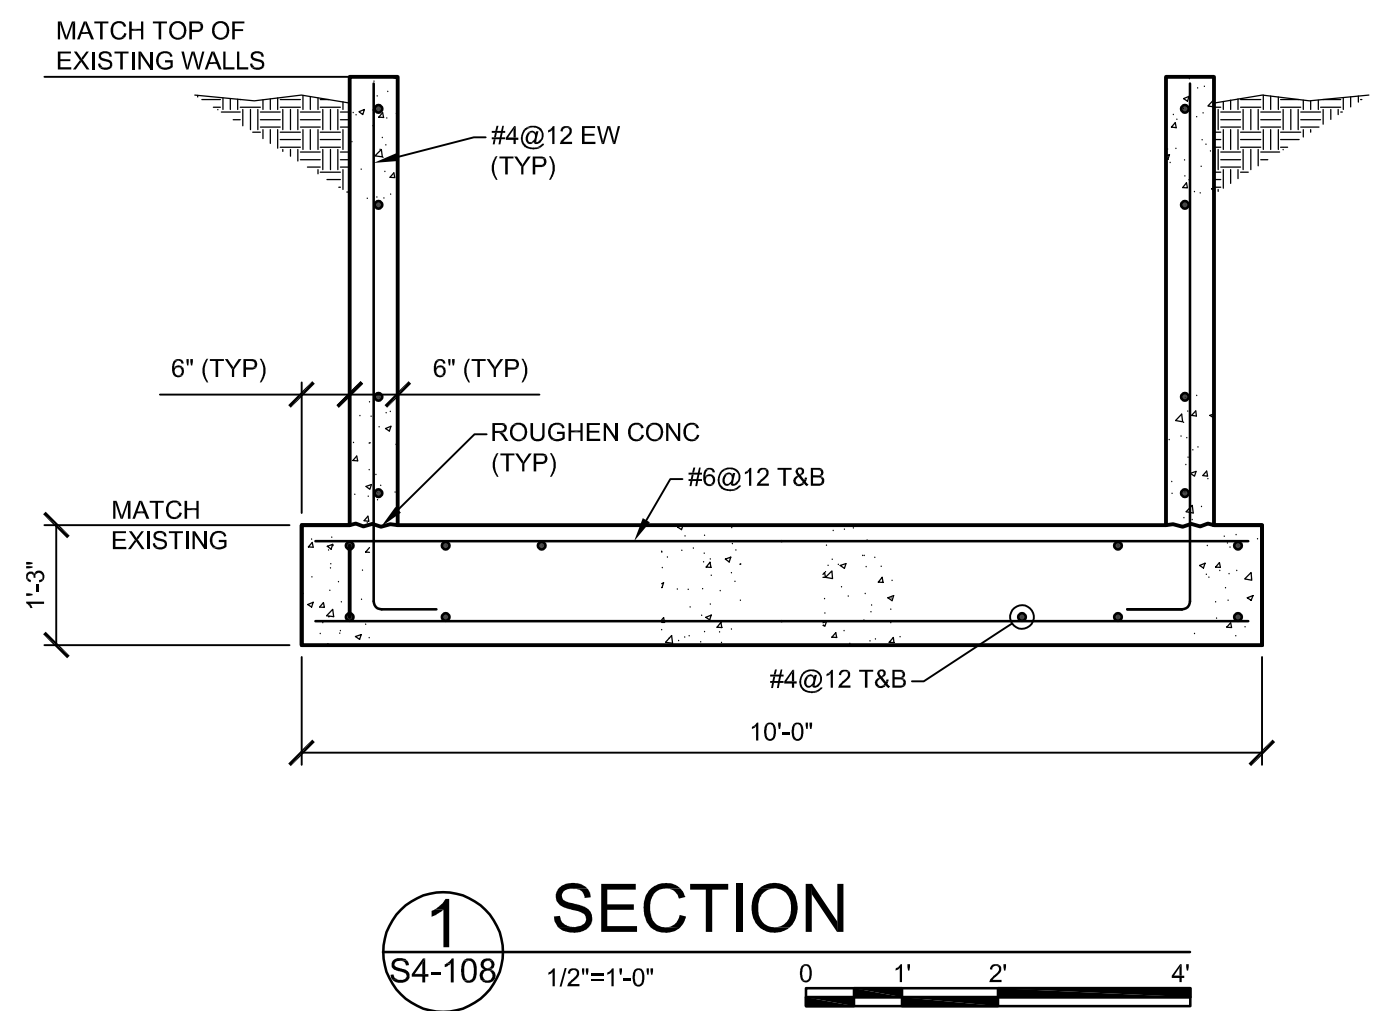

stv STV Incorporated 255 West Vaden Drive Douglassville, Pennsylvania tel: 610-385-6000 fax: 610-385-6501 www.stvinc.com		A		R. NEFF		ISSUED FOR BID	
		NO.	DATE	BY	DESCRIPTION	REVISIONS	
A-E FIRM		USDA		USDA		Agricultural Research Service	
PROJECT MANAGER		R. NEFF		N. GIRKEN		RUNOFF STATION - GRASSLAND, SOIL AND WATER RESEARCH LABORATORY (GSWRL)	
DESIGNER		S. CHAMBERS		D. SMITH		RUNOFF STATION SW17 REPAIRS	
CHECKED BY		SAFETY & HEALTH		P. JOVANOVIH		FACILITIES MODERNIZATION BRANCH (FMB)	
DRAWN BY		REAL PROPERTY		L. WURZBERGER		FACILITIES DIVISION (FD)	
R. MARTIN		DATE		SOLICITATION NO.		RIESEL S4-108	
						DWG NO.	

GENERAL SHEET NOTES

- FOR GENERAL STRUCTURAL NOTES, LEGEND, AND STRUCTURAL TECHNICAL TERMS SEE DRAWING S-001.
- FOR RUNOFF STATION LOCATION PLAN SEE DRAWING S-003.
- RESTORE GRADE TO THE EXISTING CONDITION UPON COMPLETION OF THE RETAINING WALL CONSTRUCTION.
- CRACK WIDTH= 1/8" UN.





SHEET KEYNOTES


- REMOVE STEEL BEAM AND RETURN TO OWNER.
- REMOVE EXISTING WING WALLS AND ASSOCIATED FOUNDATIONS IN THEIR ENTIRETY. IF FOUNDATIONS BEAR ON PIERS, PIERS SHALL REMAIN AND BE REUSED. ASSUME WALL EXTENDS 18" BELOW GRADE.

- ROUT CRACKS TO 3/8-INCH DEPTH, EA FACE. PREP SURFACES AND PRESSURE INJECT EPOXY FILL IN CRACKS IN WING WALLS. FOLLOW EPOXY MANUFACTURERS PREP AND INSTALLATION REQUIREMENTS.
- RECONSTRUCT RETAINING WALL AND FOUNDATION.
- INSTALL #4@12 BY 30-INCHES LONG. EPOXY ANCHOR INTO EXISTING WALL, 6-INCH EMBED.


ESTIMATED CRACK LENGTH (NTS)

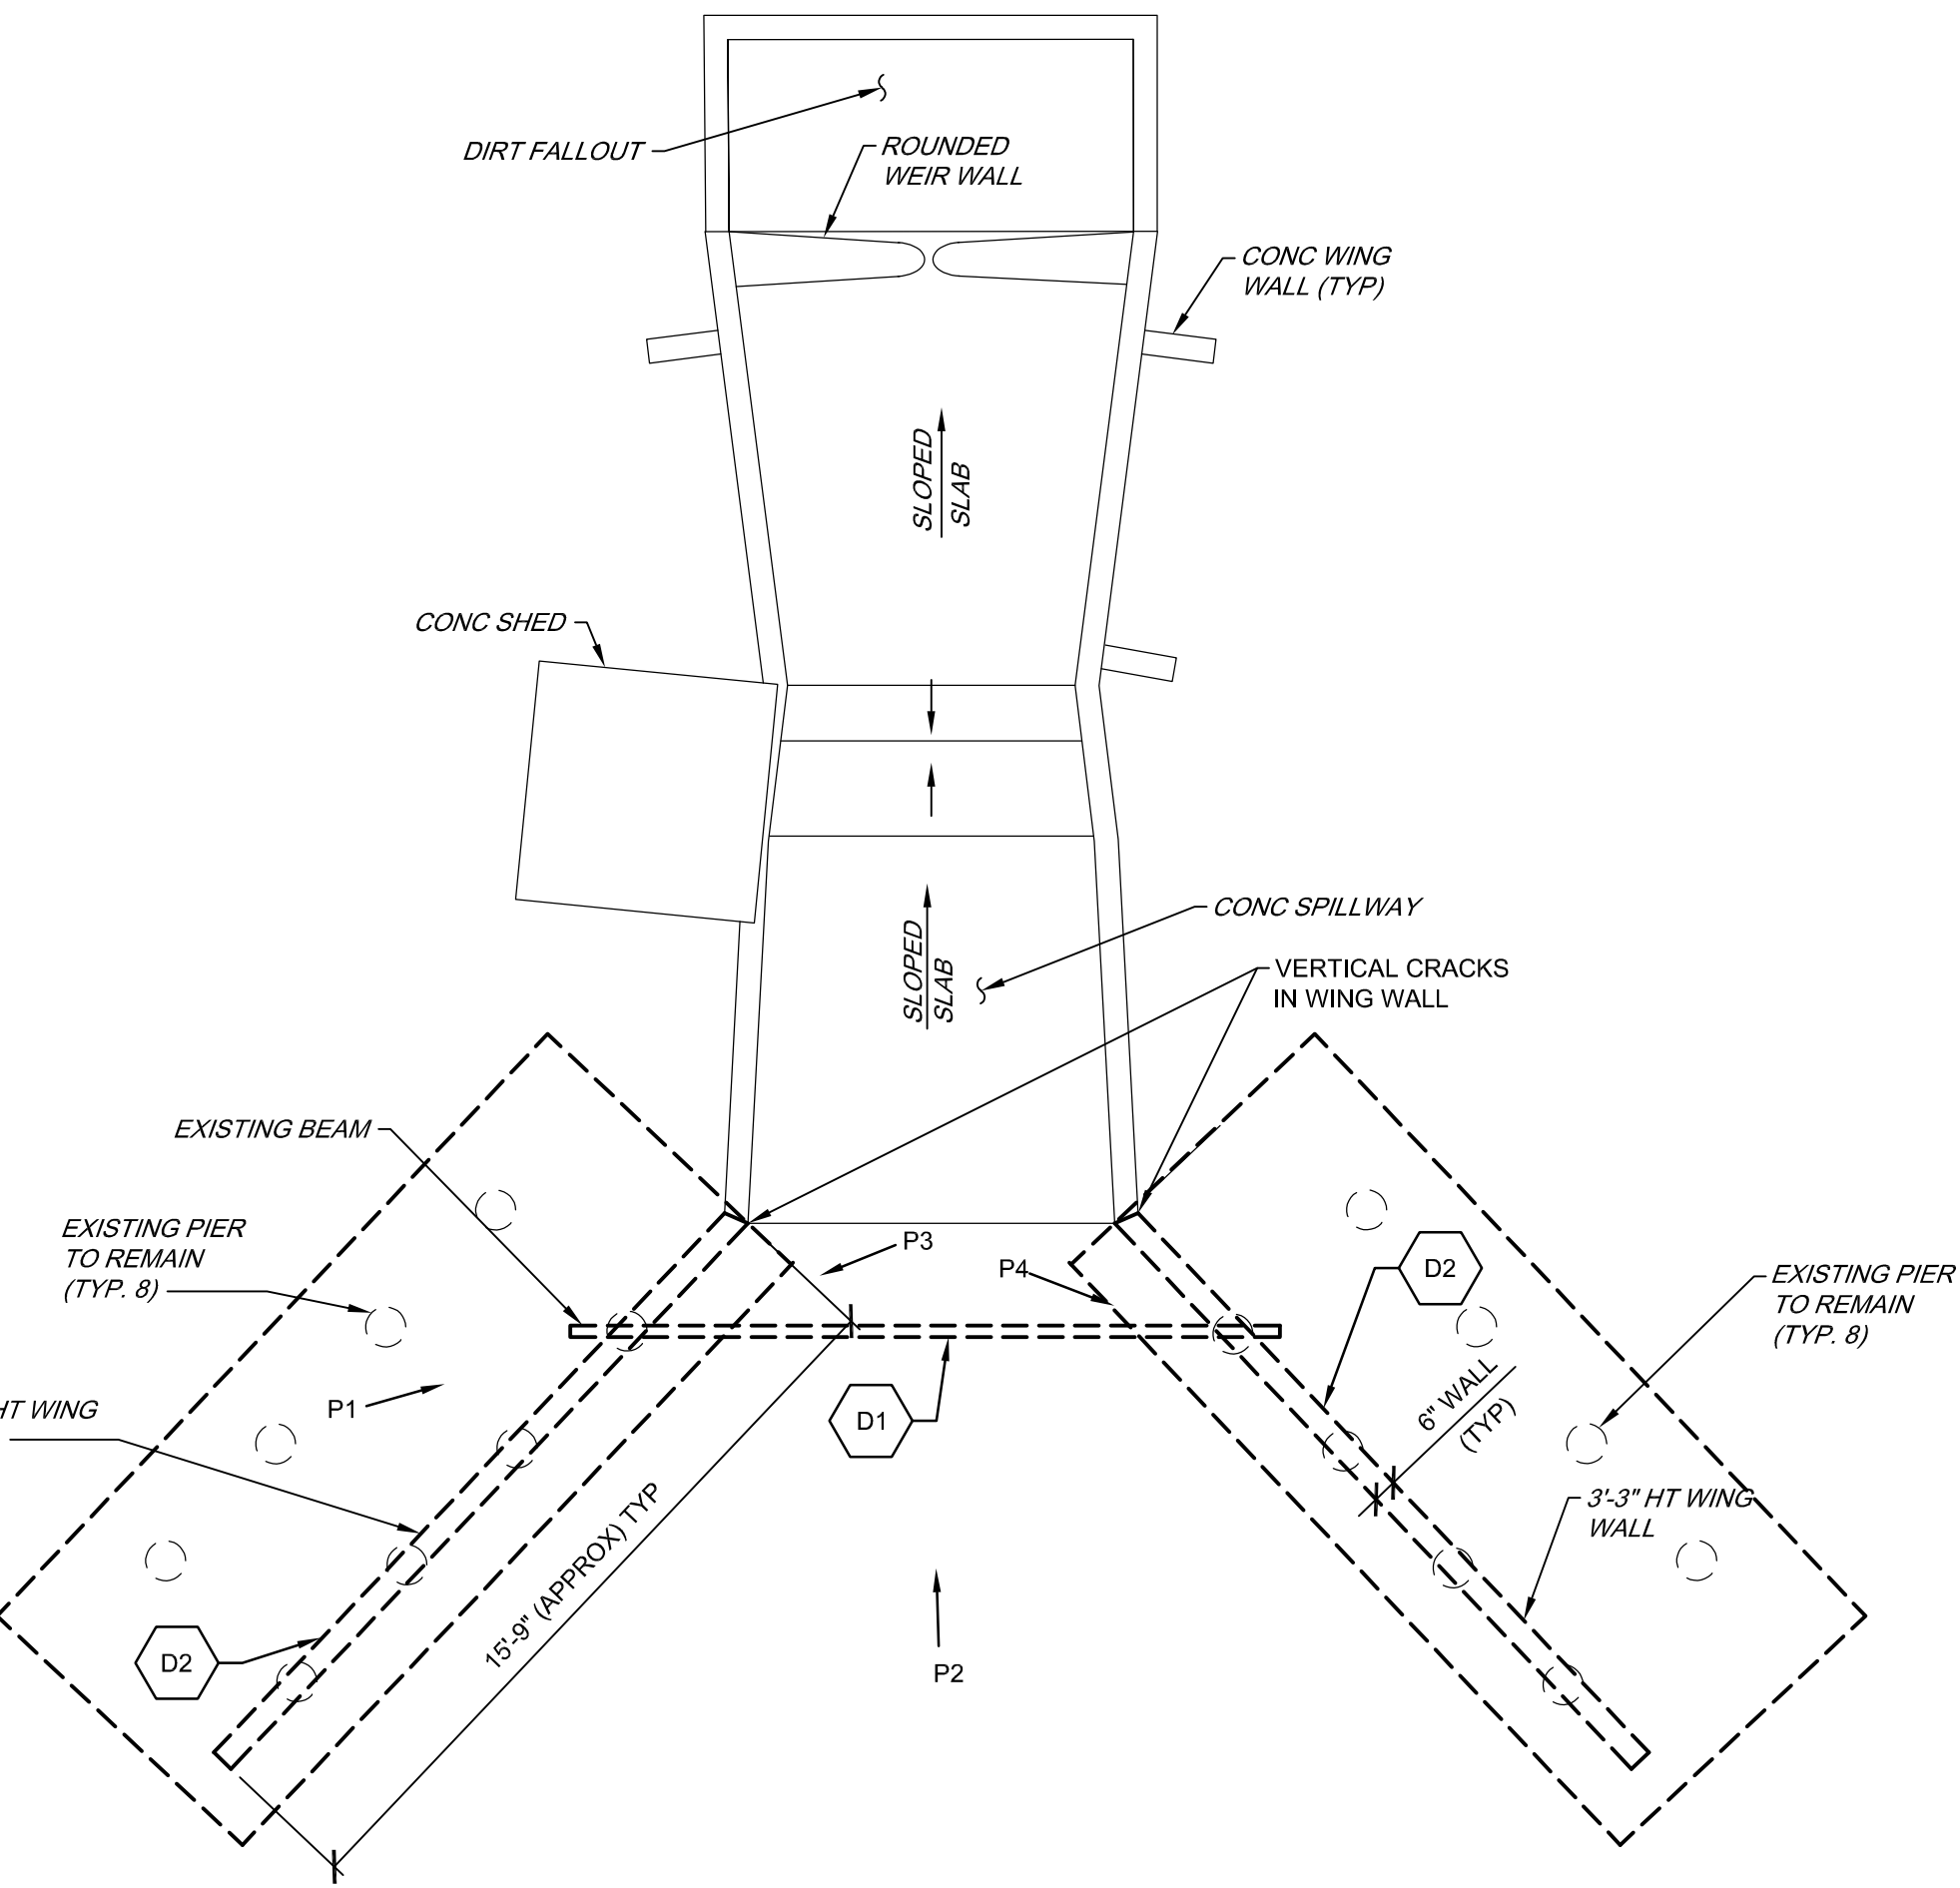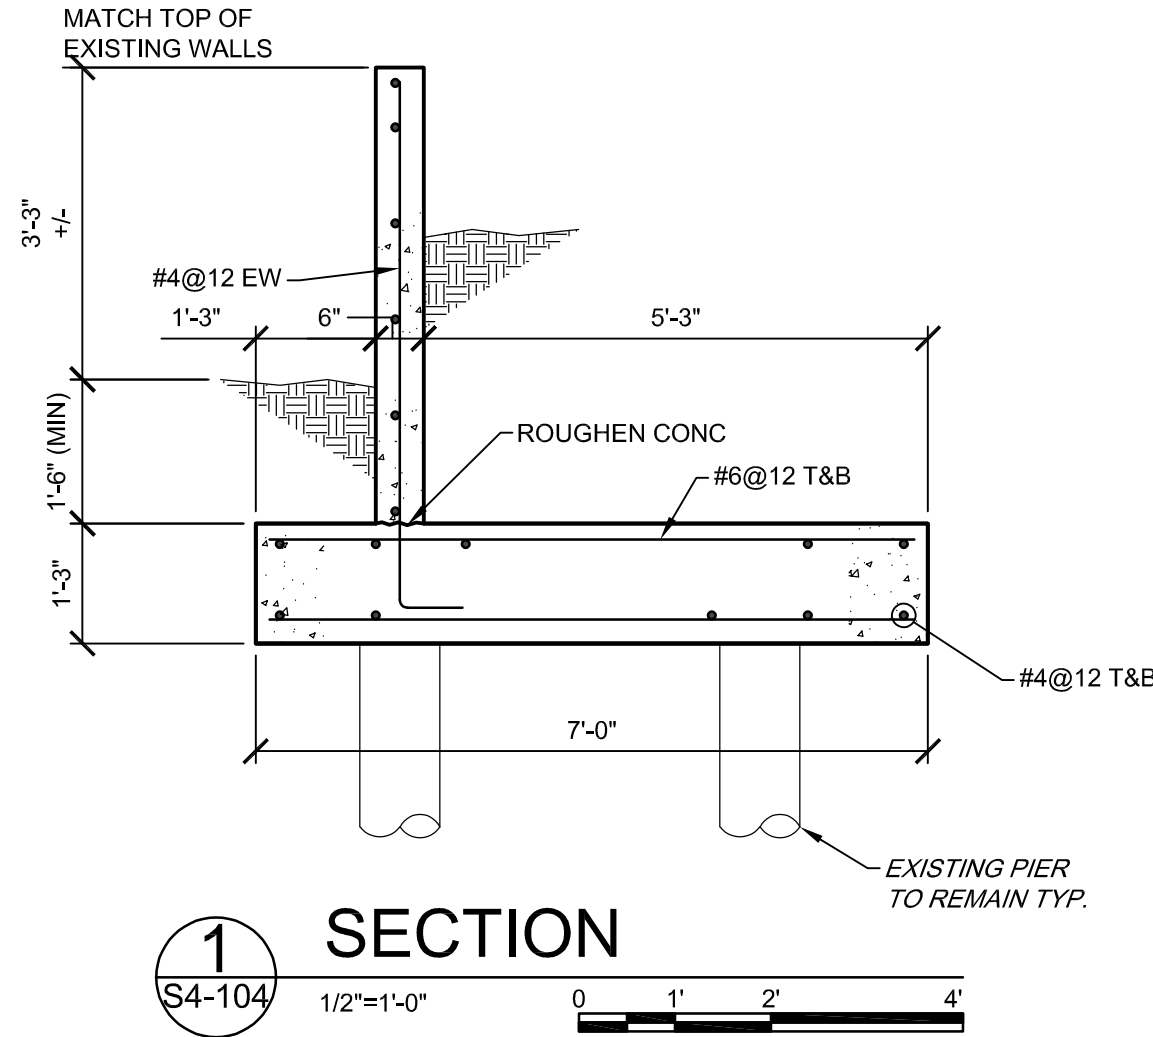

RUNOFF STATION W10 DEMOLITION PLAN

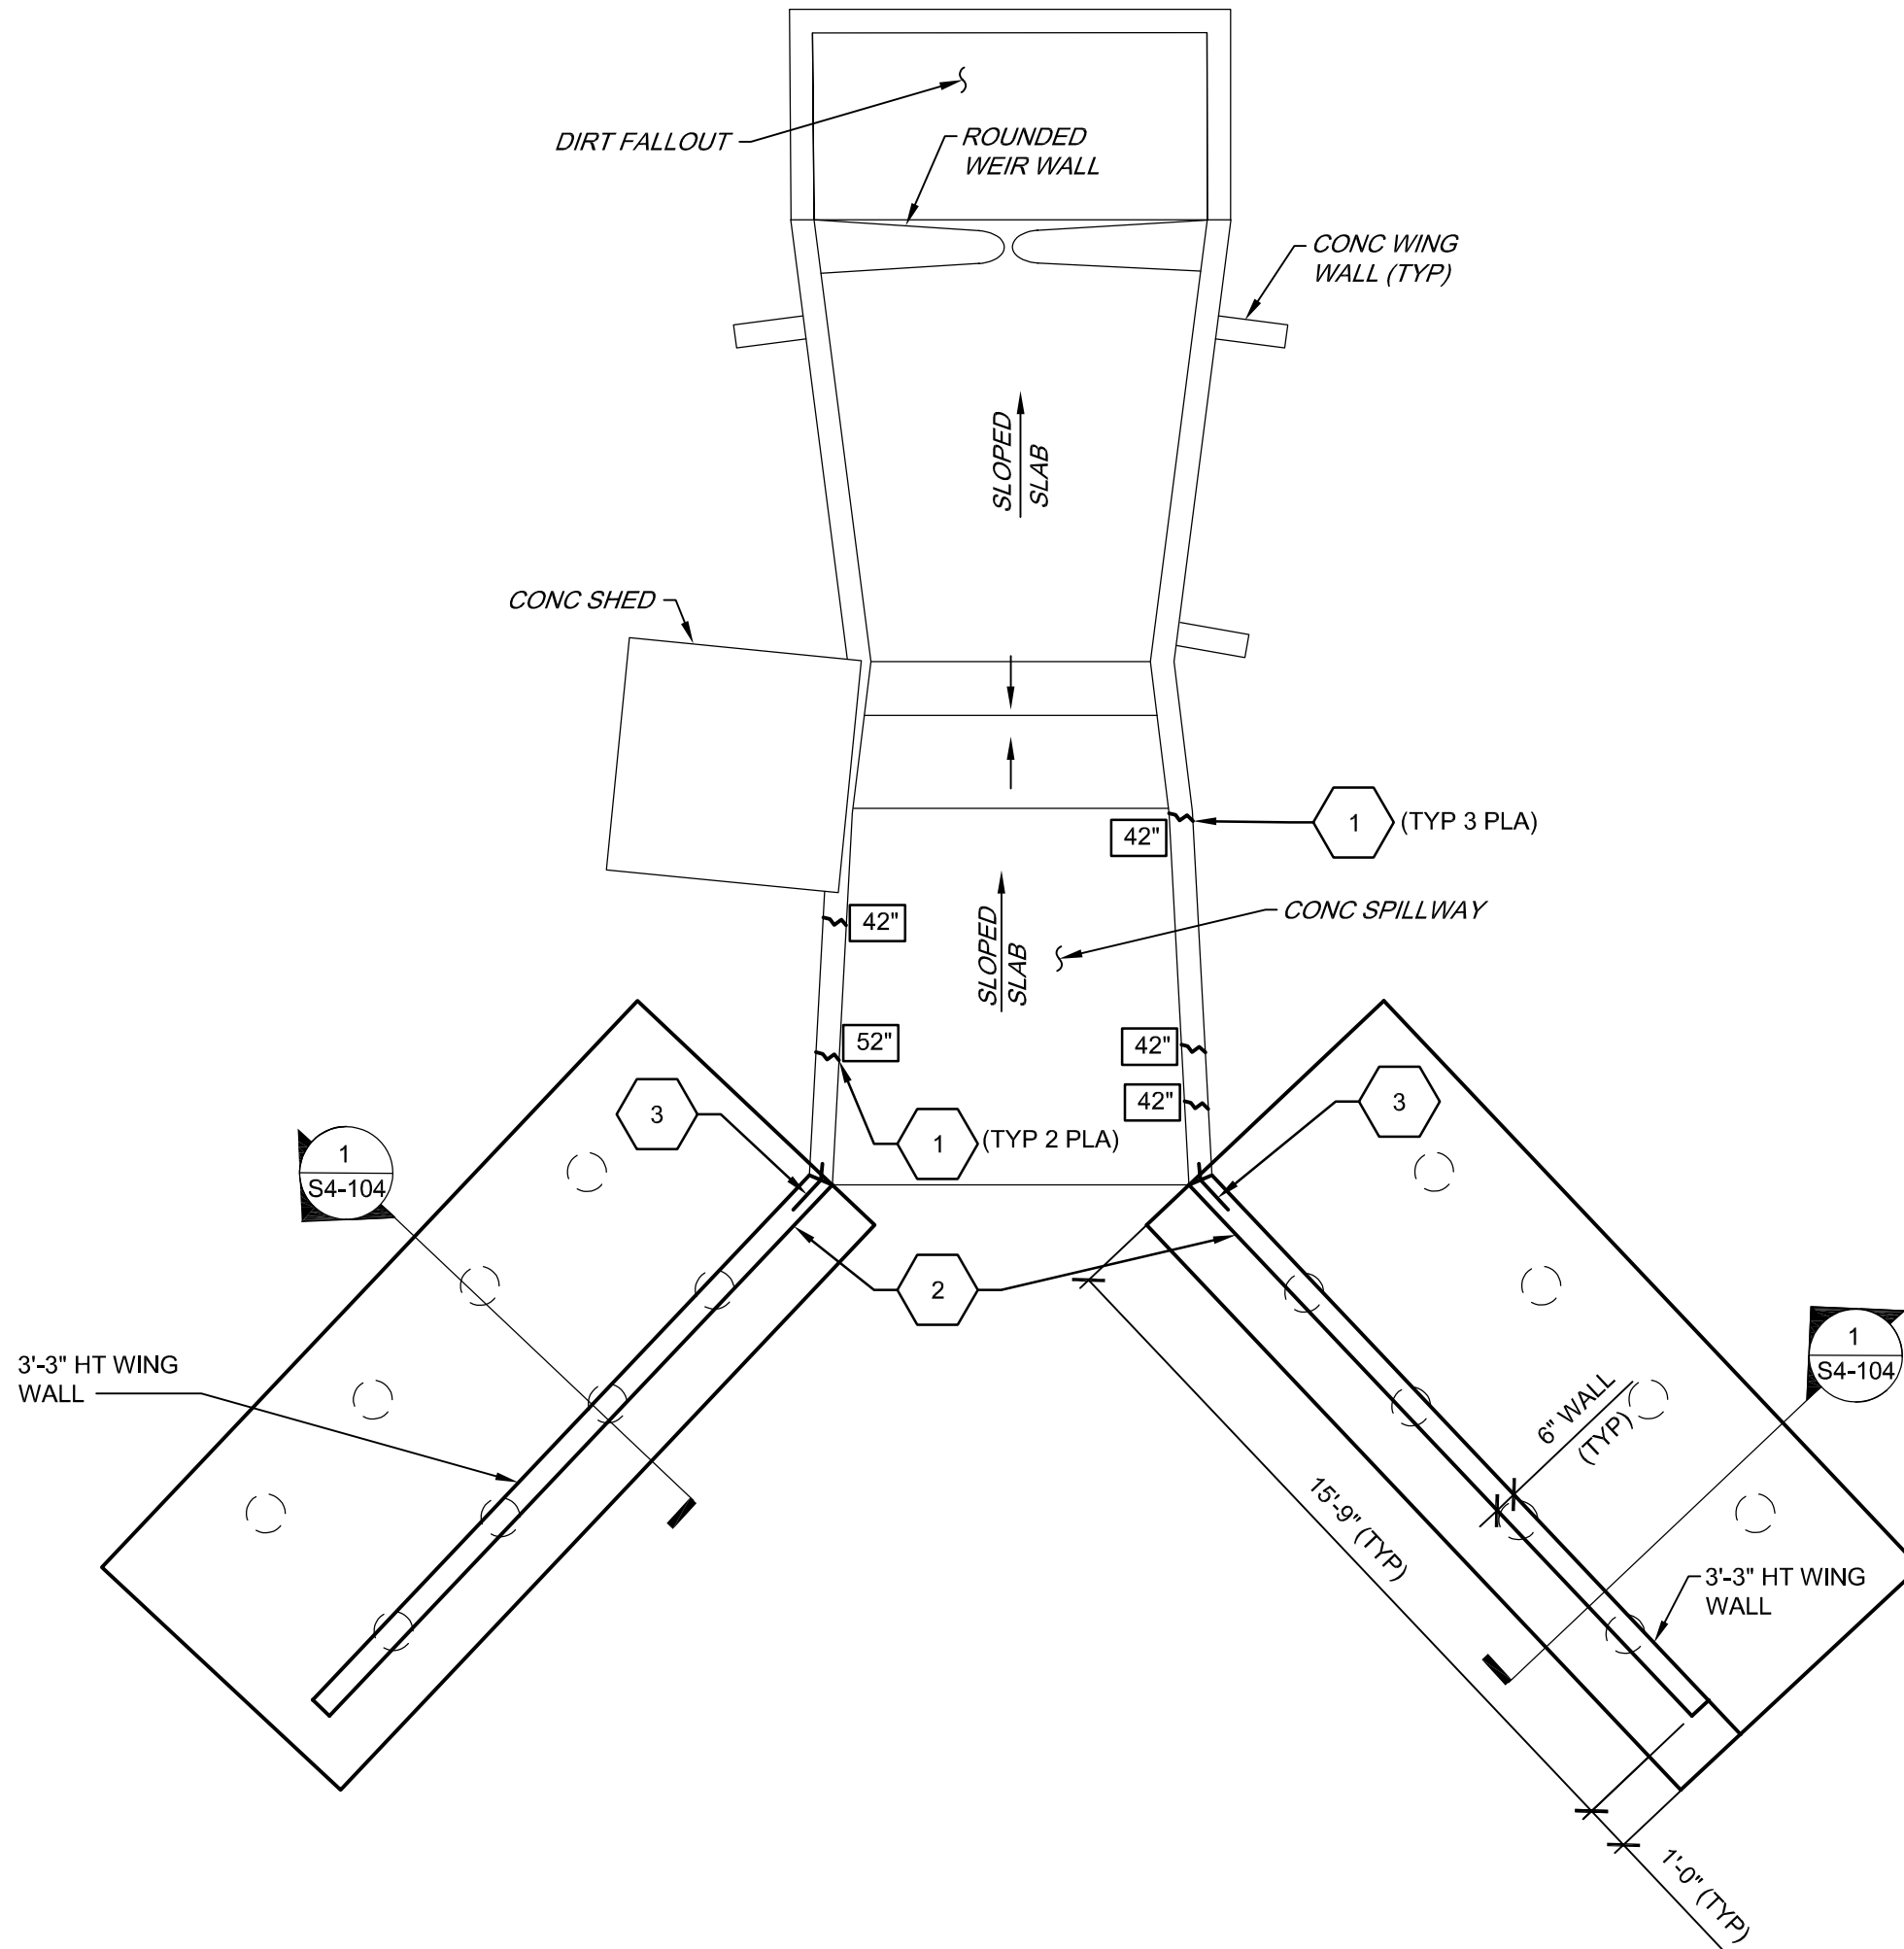


RUNOFF STATION W10 NEW WORK PLAN

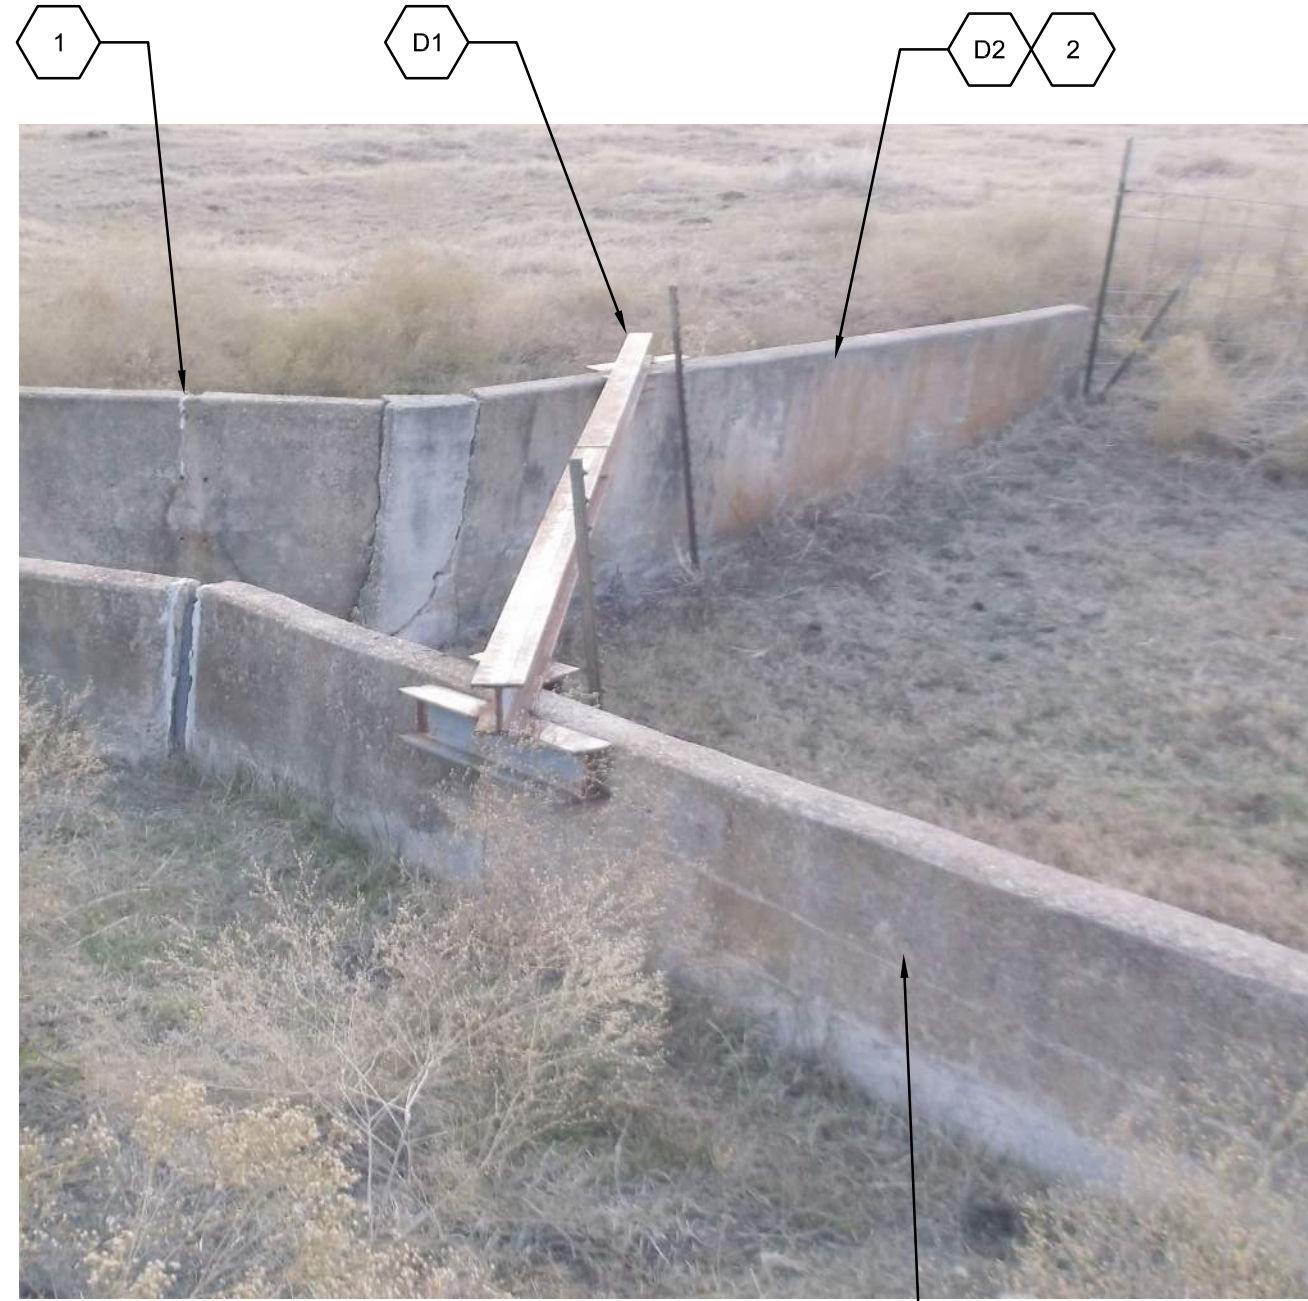


P1



P2

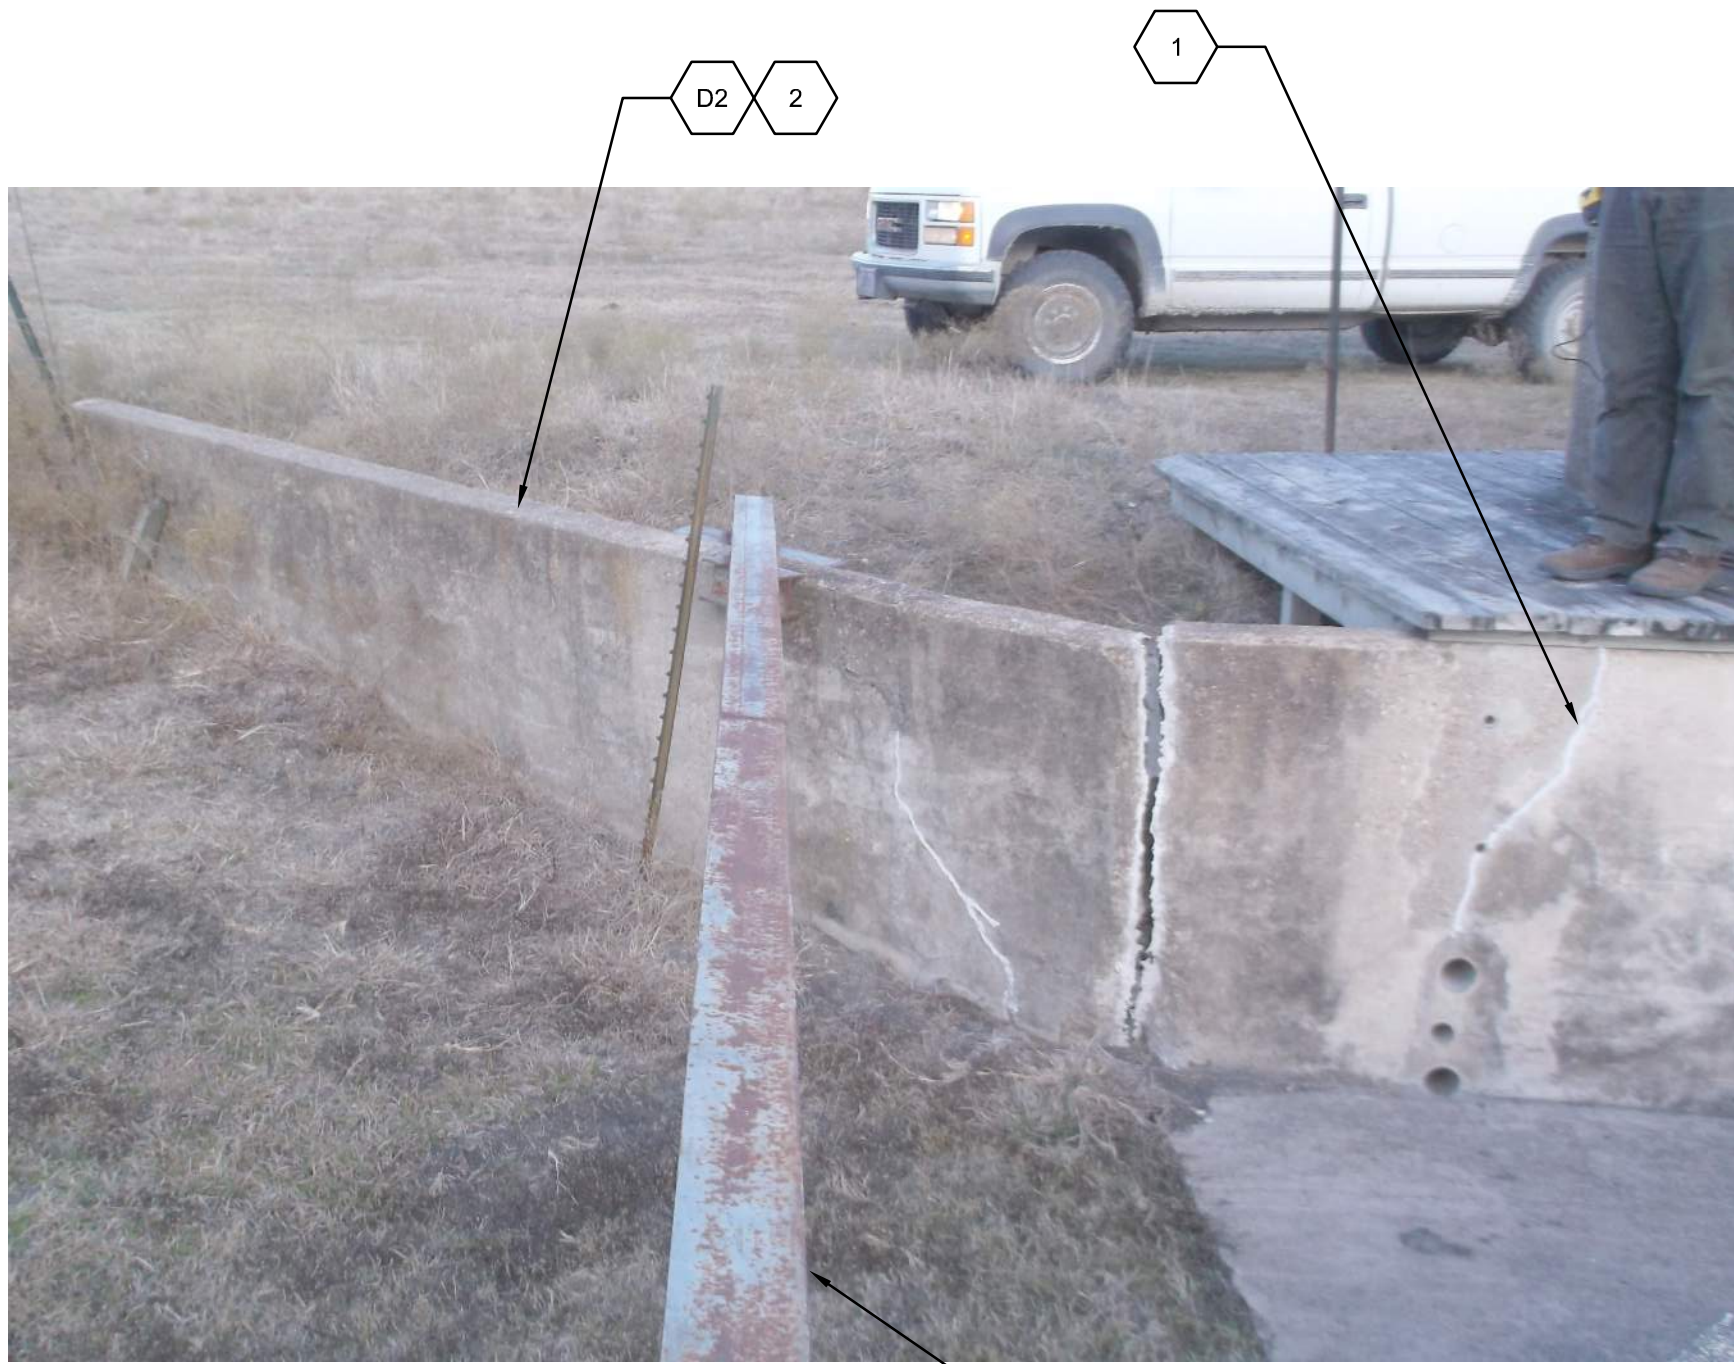

P3

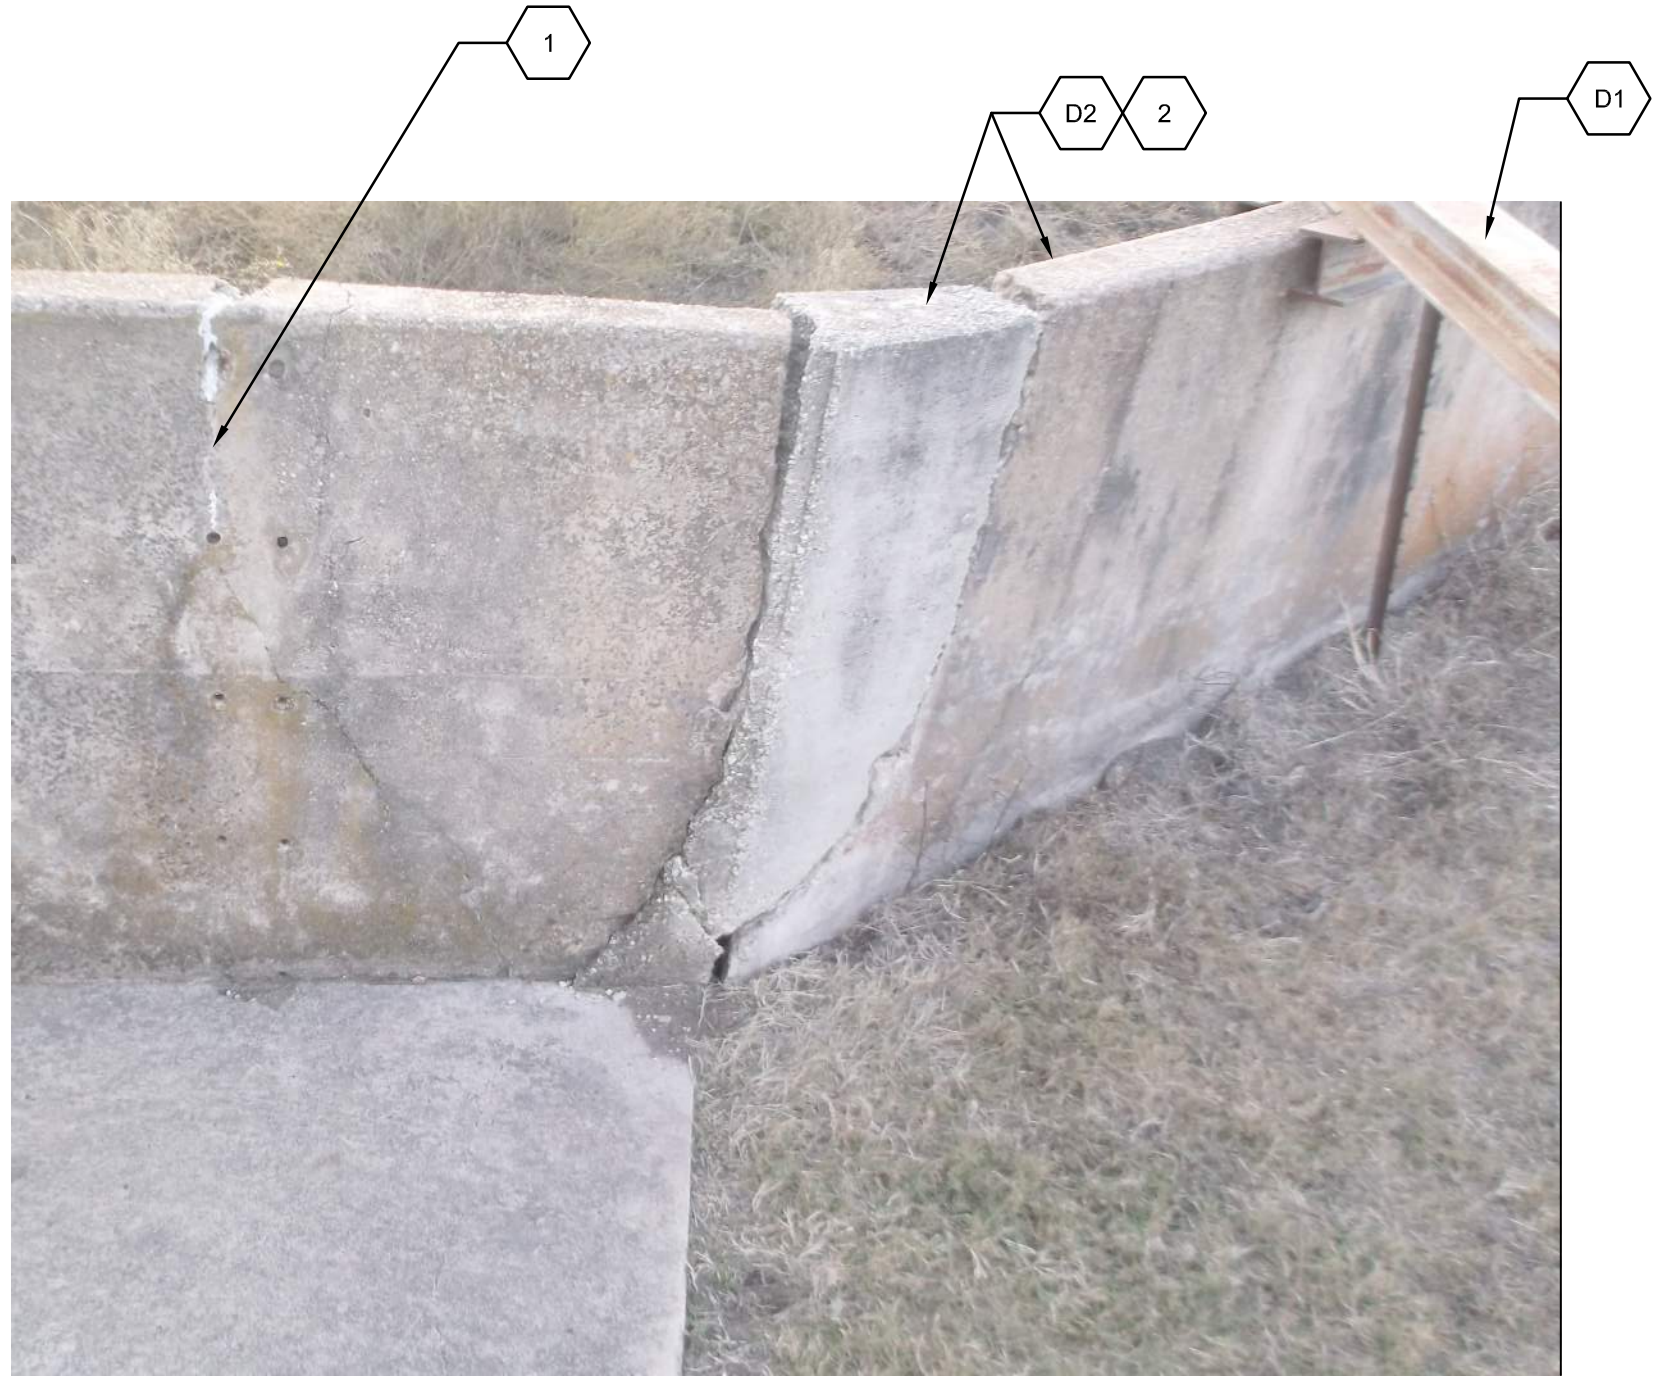

P4

STV

STV Incorporated
255 West Vaden Drive
Douglassville, Pennsylvania
tel: 610-385-4500 fax: 610-385-4501
www.stvinc.com

A-E FIRM USDA

PROJECT MANAGER EFM

R. NEFF N. GIRKEN

DESIGNER LM

S. CHAMBERS D. SMITH

CHECKED BY S. CHAMBERS

DRAWN BY R. MARTIN

SAFETY & HEALTH P. JOVANOVIH

REAL PROPERTY L. WURZBERGER

NO. DATE BY DESCRIPTION

REVISIONS

U
S
D
A

Agriultural Research Service

RUNOFF STATION - GRASSLAND, SOIL AND WATER RESEARCH LABORATORY (GSWRL)
1702 BACKLICK ROAD, RIESEL, TEXAS 76868

RUNOFF STATION W10 REPAIRS

SOLICITATION NO. FACILITIES MODERNIZATION BRANCH (FMB) FACILITIES DIVISION (FD) RIESEL S4-104

DATE DWG NO.