



1. FOR GENERAL STRUCTURAL NOTES, LEGEND, AND STRUCTURAL TECHNICAL TERMS SEE DRAWING S-001.

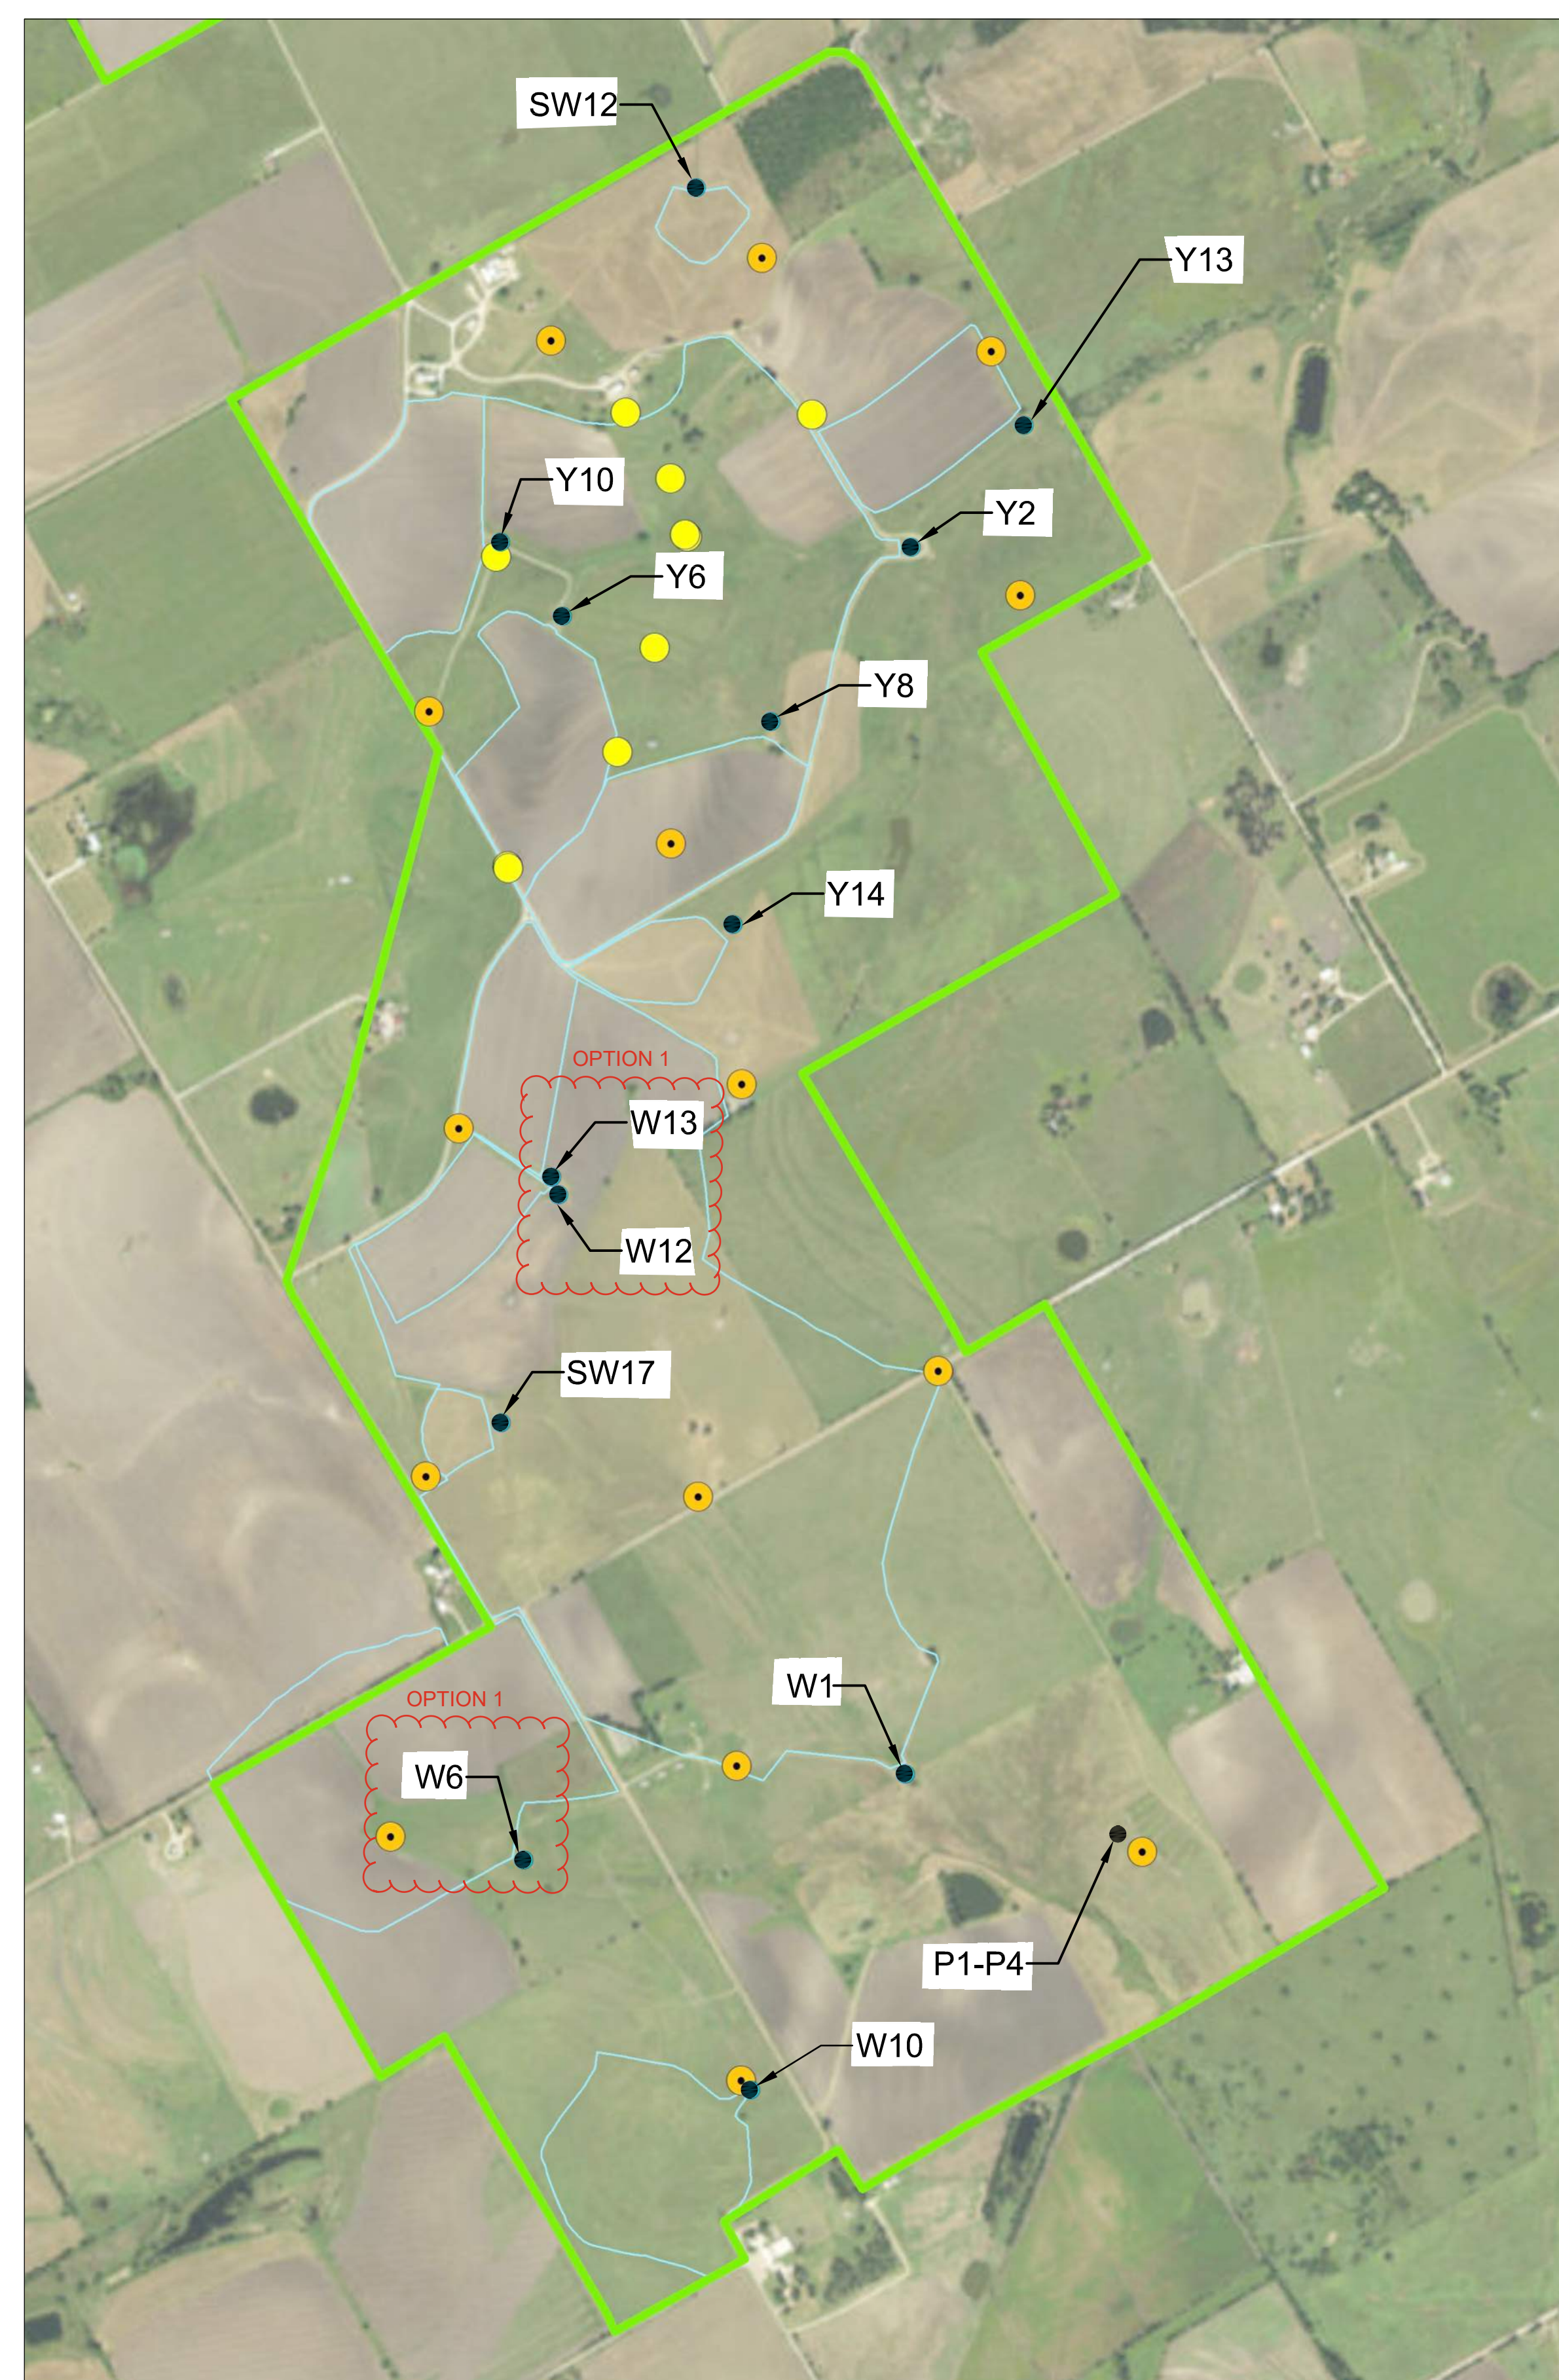


RUNOFF STATIONS LOCATION PLAN

SCALE: 1"=700'

							
STV Incorporated 205 West Walnut Drive Douglasville, Pennsylvania tel: 610-385-6200 fax: 610-385-5501 www.stvnc.com		A	12/22/23	R. NEFF	ISSUED FOR BID		
		NO.	DATE	BY	DESCRIPTION		
					REVISIONS		
		U S D A			Agricultural Research Service		
					RUNOFF STATION - GRASSLAND, SOIL AND WATER RESEARCH LABORATORY (GSWRL)		
					1702 BACKLICK ROAD, REESEL, TEXAS 79662		
A-E FIRM	USDA			RUNOFF STATIONS LOCATION PLAN			
PROJECT MANAGER	EPM	SOLICITATION NO.		FACILITIES MODERNIZATION BRANCH (FMB)		REESEL S-003	
R. NEFF	M. GIRKEN			FACILITIES DIVISION (FD)			
DESIGNER	LM			4601 GUNNERSBY AVENUE			
S. CHAMBERS	D. SMITH			BELTSVILLE, MD 20705			
CHECKED BY	SAFETY & HEALTH						
M. HIGH	P. JOVANOVICH						
DRAWN BY	REAL PROPERTY	DATE					
W. HELLER	L. WURZBERGER						

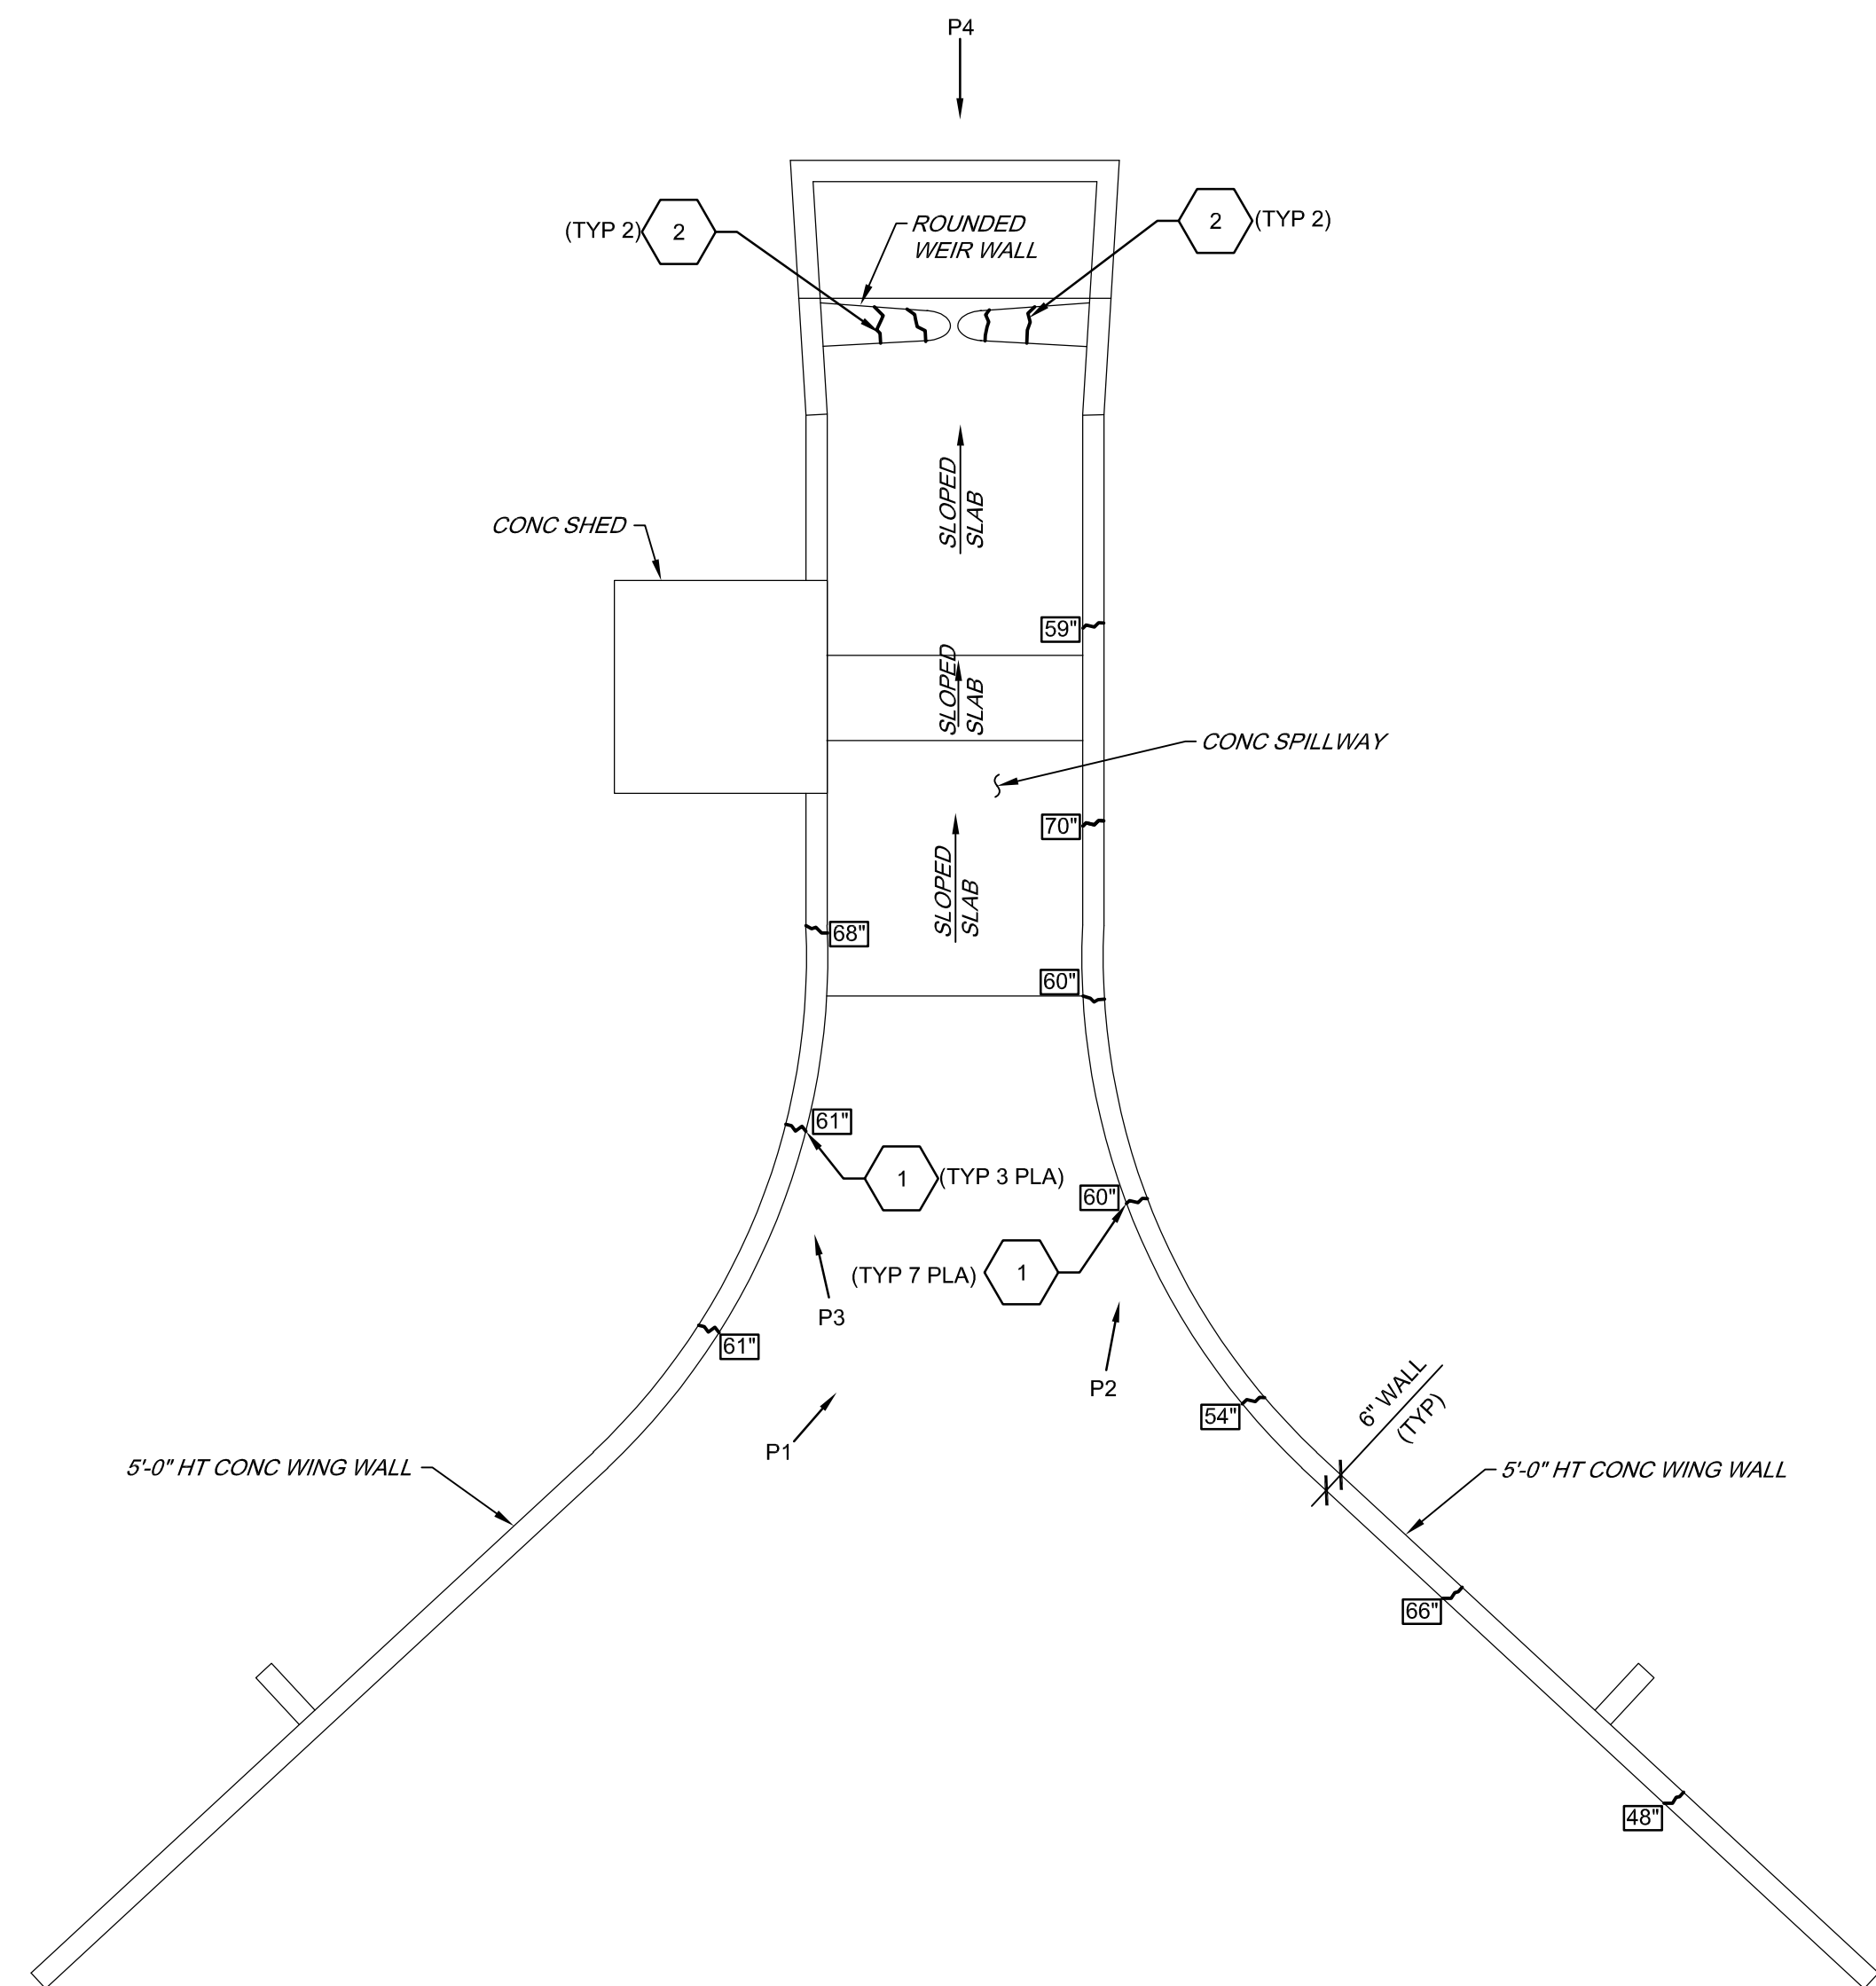

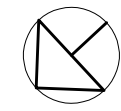
 **RUNOFF STATION W6 NEW WORK PLAN**
1/4"=1'-0" 0 2' 4' 8'



P1



P2

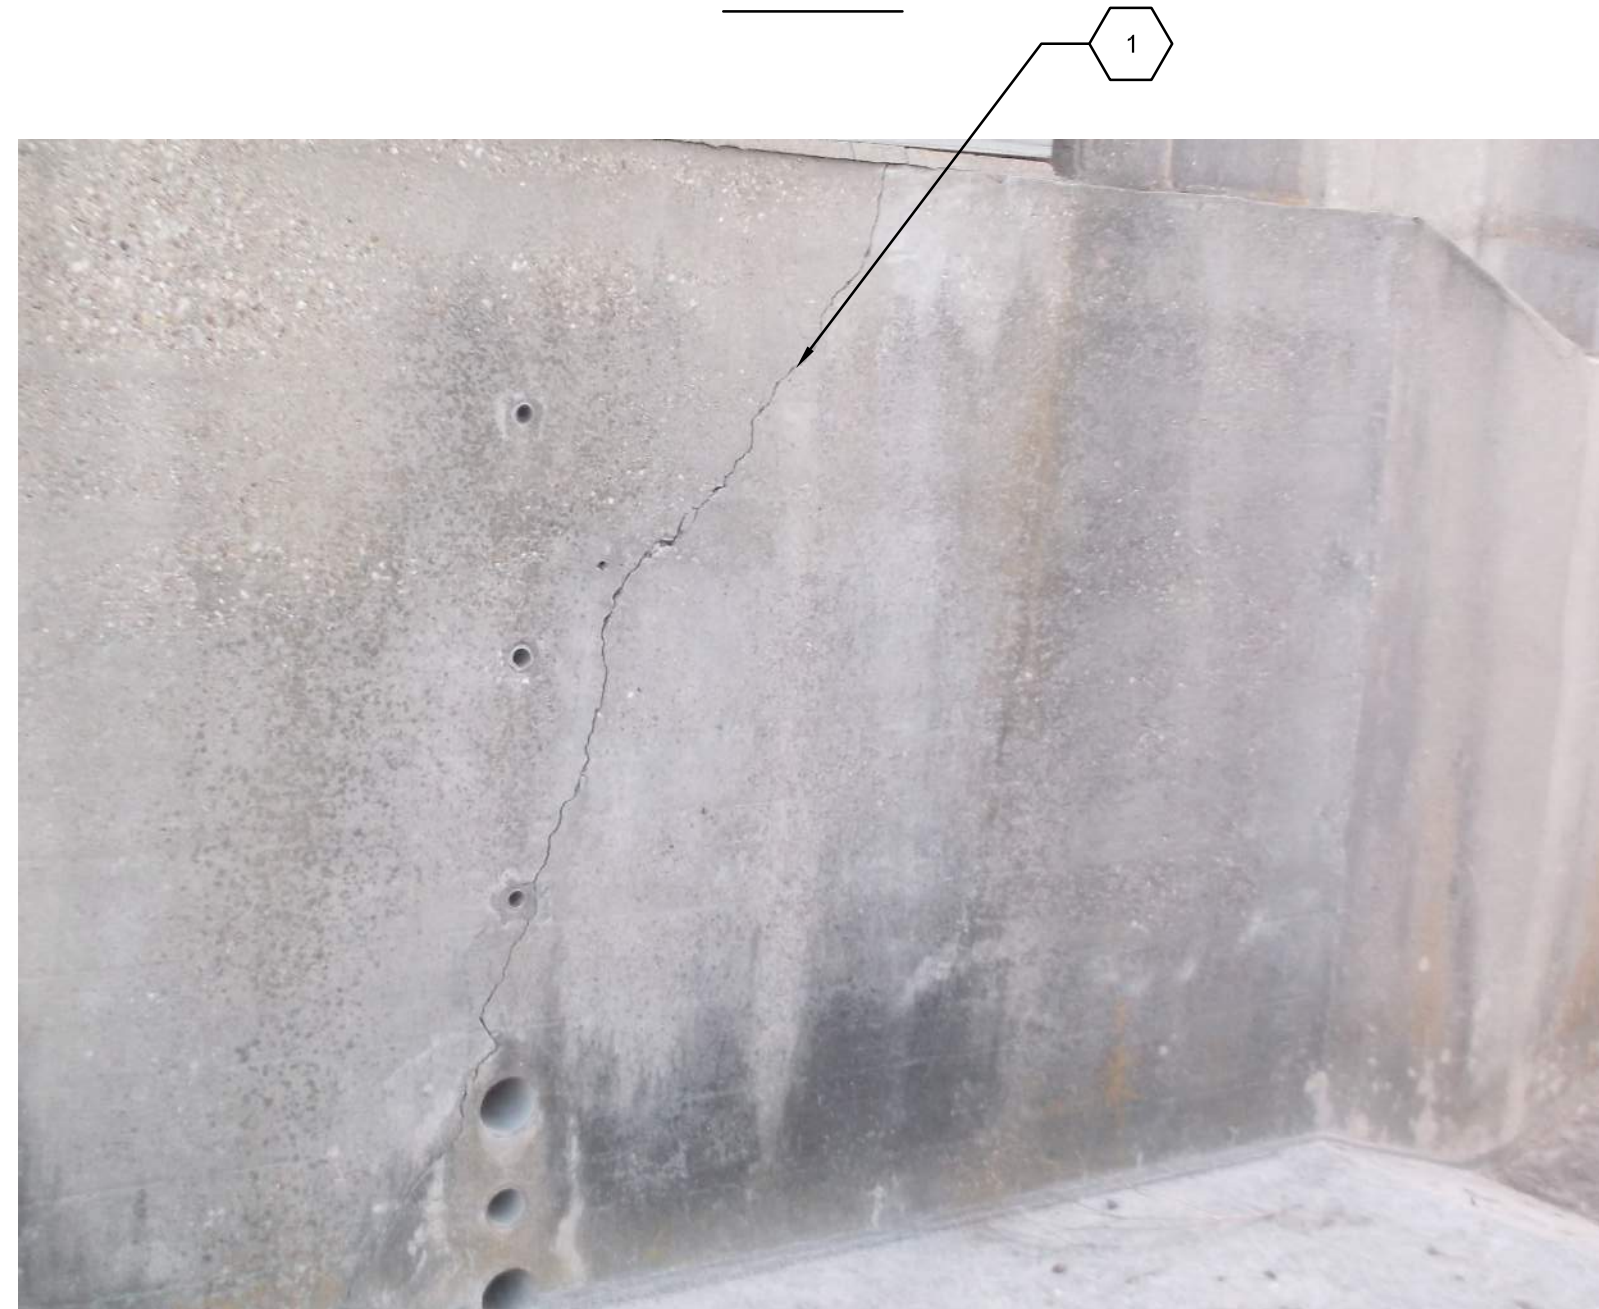


P3



P4

GENERAL SHEET NOTES

1. FOR GENERAL STRUCTURAL NOTES, LEGEND, AND STRUCTURAL TECHNICAL TERMS SEE DRAWING S-001.
2. FOR RUNOFF STATION LOCATION PLAN SEE DRAWING S-003.
3. CRACK WIDTH $\frac{1}{8}$ " UNO

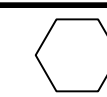

SHEET KEYNOTES

1. ROUT CRACKS TO 3/8-INCH DEPTH, EA FACE. PREP SURFACES AND PRESSURE INJECT EPOXY FILL IN CRACKS IN WING WALLS. FOLLOW EPOXY MANUFACTURERS PREP AND INSTALLATION REQUIREMENTS.
2. ROUT CRACKS IN WEIR, PREP SURFACES AND PRESSURE INJECT EPOXY FILL IN CRACKS. INSTALL BITUTHENE LIQUID MEMBRANE, AS MANUFACTURED BY GRACE CONSTRUCTION PRODUCTS, OR APPROVED EQUAL, AT ALL JOINTS.

 ESTIMATED CRACK LENGTH (NTS)



STV Incorporated
255 West Vaden Drive
Douglassville, Pennsylvania
tel: 610-385-6000 fax: 610-385-6501
www.stvinc.com

A-E FIRM USDA

PROJECT MANAGER EFM

R. NEFF N. GIRKEN

DESIGNER LM

S. CHAMBERS D. SMITH

CHECKED BY SAFETY & HEALTH

XXXX P. JOVANOVI

DRAWN BY REAL PROPERTY

W. HELLER L. WURZBERGER

NO. DATE BY DESCRIPTION

REVISIONS

U S D A

Agriultural Research Service

RUNOFF STATION - GRASSLAND, SOIL AND WATER RESEARCH LABORATORY (GSWRL)

1700 BLACKLAND ROAD, RIESEL, TEXAS 76882

RUNOFF STATION

W6

REPAIRS

SOLICITATION NO.


FACILITIES MODERNIZATION BRANCH (FMB)

FACILITIES DIVISION (FD)

9001 SUNNYSIDE AVENUE
SELTOVILLE, MO 30105

RIESEL S4-103

DWG NO.

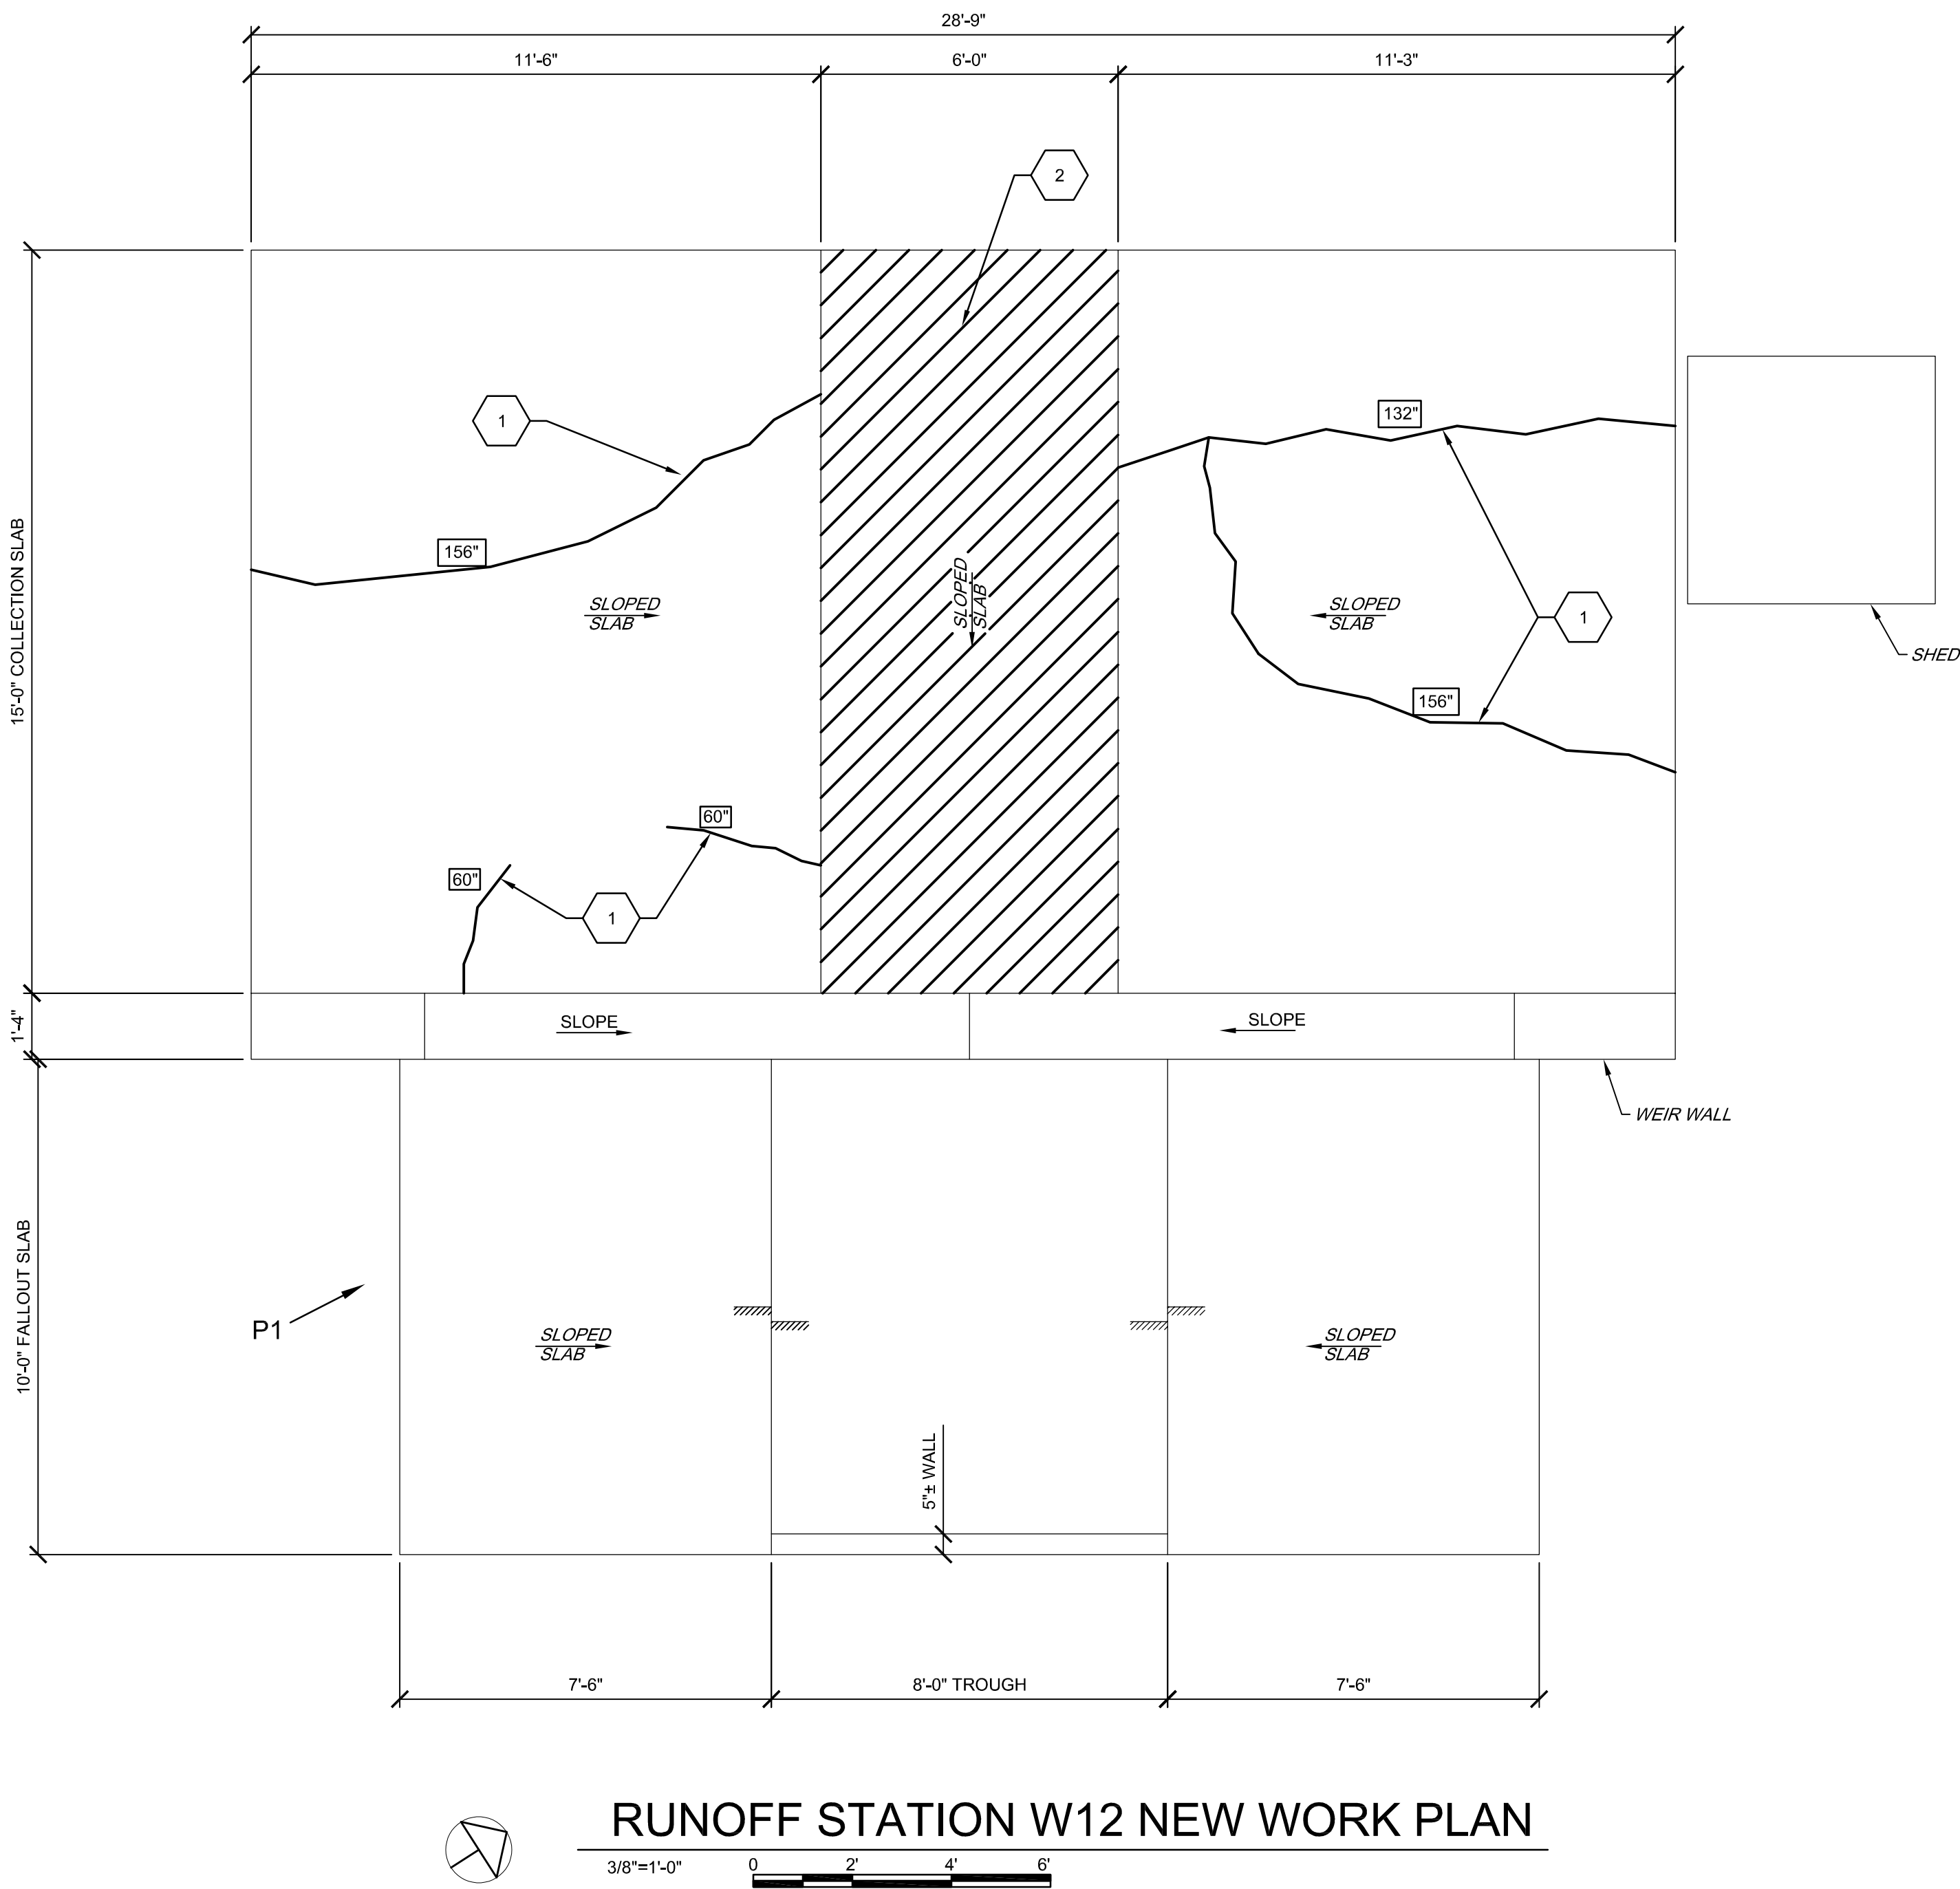


P1




P2

GENERAL SHEET NOTES			
1.	FOR GENERAL STRUCTURAL NOTES, LEGEND, AND STRUCTURAL TECHNICAL TERMS SEE DRAWING S-001.		
2.	FOR RUNOFF STATION LOCATION PLAN SEE DRAWING S-003.		
3.	CRACK WIDTH = 1/8" UN.		
SHEET KEYNOTES			
1.	ROUT CRACKS IN SLAB TO 3/8-INCH DEPTH. PREP SURFACES AND PRESSURE INJECT EPOXY FILL IN CRACKS. FOLLOW EPOXY MANUFACTURERS PREP AND INSTALLATION REQUIREMENTS.		
2.	REMOVE EXISTING SLAB TO 1" DEPTH. PREPARE SURFACE AND INSTALL POLYMER MODIFIED TOPPING SLAB TO RE-ESTABLISH SLAB SURFACE AND ELEVATION. FOLLOW TOPPING SLAB MANUFACTURERS REQUIREMENTS FOR SURFACE PREP AND TOPPING INSTALLATION.		
# ESTIMATED CRACK LENGTH (NTS)			

 STV Incorporated 255 West Walsh Drive Douglassville, Pennsylvania tel: 610-385-6000 fax: 610-385-6501 www.stvinc.com																							
A		12/22/23		R. NEFF		ISSUED FOR BID																	
NO.		DATE		BY		DESCRIPTION																	
						REVISIONS																	
						Agriscience Research Service																	
						RUNOFF STATION - GRASSLAND, SOIL AND WATER RESEARCH LABORATORY (GSWR)																	
						1702 BLACKHORN ROAD, RIESEL, TEXAS 79682																	
						RUNOFF STATION W12 REPAIRS																	
A-E FIRM		USDA																					
PROJECT MANAGER		EPH																					
R. NEFF		N. GIRKEN																					
DESIGNER		LM																					
S. CHAMBERS		D. SMITH																					
CHECKED BY		SAFETY & HEALTH																					
S. CHAMBERS		P. JOVANOVIH																					
DRAWN BY		REAL PROPERTY																					
R. MARTIN		L. WURZBERGER																					
SOLICITATION NO.				FACILITIES MODERNIZATION BRANCH (FMB) FACILITIES DIVISION (FD)				RIESEL S4-105															
DATE				5601 SUNNYSIDE AVENUE BELLTOWNE, MO 20756				DWG NO.															

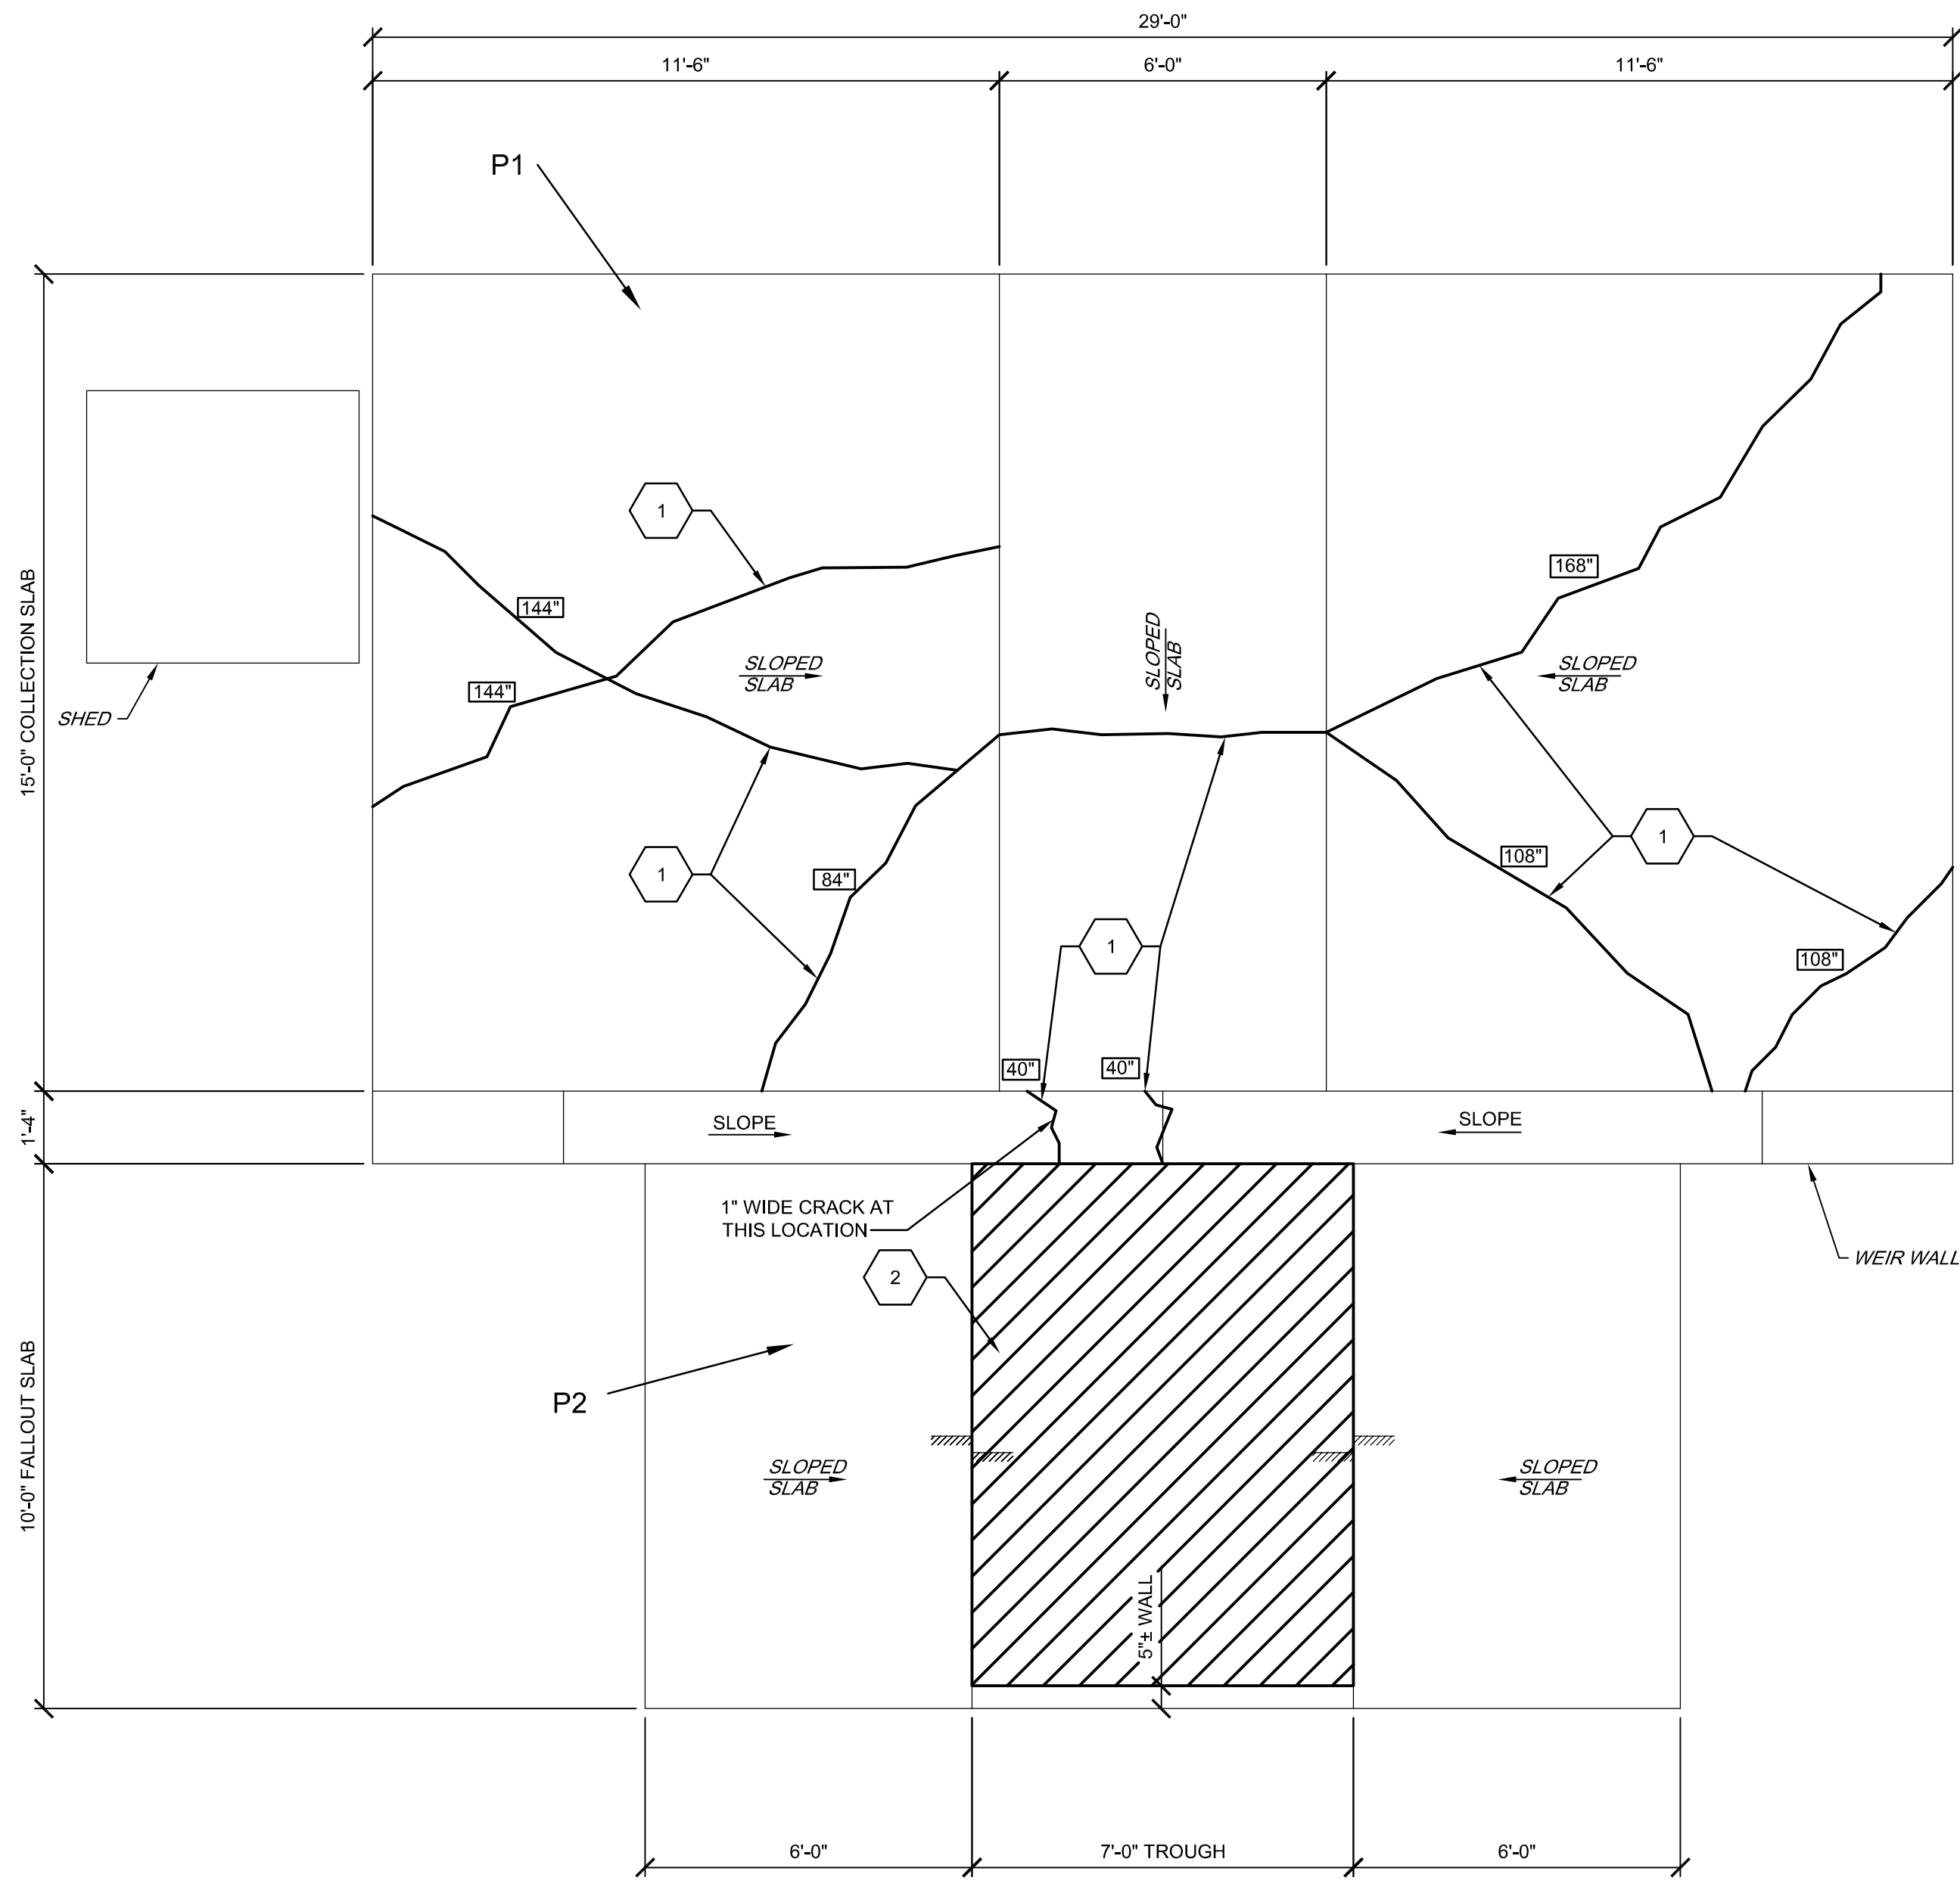

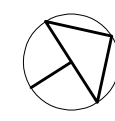 **RUNOFF STATION W13 NEW WORK PLAN**
3/8"=1'-0" 0 2' 4' 6'



P1



P2

GENERAL SHEET NOTES

- FOR GENERAL STRUCTURAL NOTES, LEGEND, AND STRUCTURAL TECHNICAL TERMS SEE DRAWING S-001.
- FOR RUNOFF STATION LOCATION PLAN SEE DRAWING S-003.
- CRACK WIDTH" = 1/8 UN.



SHEET KEYNOTES

- ROUT CRACKS IN SLAB AND WEIR TO 3/8-INCH DEPTH. PREP SURFACES AND PRESSURE INJECT EPOXY FILL IN CRACKS. FOLLOW EPOXY MANUFACTURERS PREP AND INSTALLATION REQUIREMENTS. AFTER ROUT AND EPOXY, INSTALL BITUTHENE LIQUID MEMBRANE, AS MANUFACTURED BY GRACE CONSTRUCTION PRODUCTS, OR APPROVED EQUAL, AT ALL WEIR JOINTS.
- REMOVE EXISTING SLAB TO 1" DEPTH. PREPARE SURFACE AND INSTALL POLYMER MODIFIED TOPPING SLAB TO RE-ESTABLISH SLAB SURFACE AND ELEVATION. FOLLOW TOPPING SLAB MANUFACTURERS REQUIREMENTS FOR SURFACE PREP AND TOPPING INSTALLATION.

ESTIMATED CRACK LENGTH (NTS)

stv

STV Incorporated
255 West Vaden Drive
Douglassville, Pennsylvania
tel: 610-385-6000 fax: 610-385-6501
www.stvinc.com

A-E FIRM USDA

PROJECT MANAGER EPM

R. NEFF N. GIRKEN

DESIGNER LM

S. CHAMBERS D. SMITH

CHECKED BY SAFETY & HEALTH

S. CHAMBERS P. JOVANOVI

DRAWN BY REAL PROPERTY

R.MARTIN L. WURZBERGER

A 12/22/23 R. NEFF ISSUED FOR BID

NO. DATE BY DESCRIPTION

REVISIONS

USDA

Aggricultural Research Service

RUNOFF STATION - GRASSLAND, SOIL AND WATER RESEARCH LABORATORY (GSWRL)

1702 BLACKLAND ROAD, RIESEL, TEXAS 76868

RUNOFF STATION W13

REPAIRS

SOLICITATION NO.

FACILITIES MODERNIZATION BRANCH (FMB) FACILITIES DIVISION (FD)

5901 SUNNYSIDE AVENUE SEATTLE, WA 98105

RIESEL S4-106

DWG NO.