


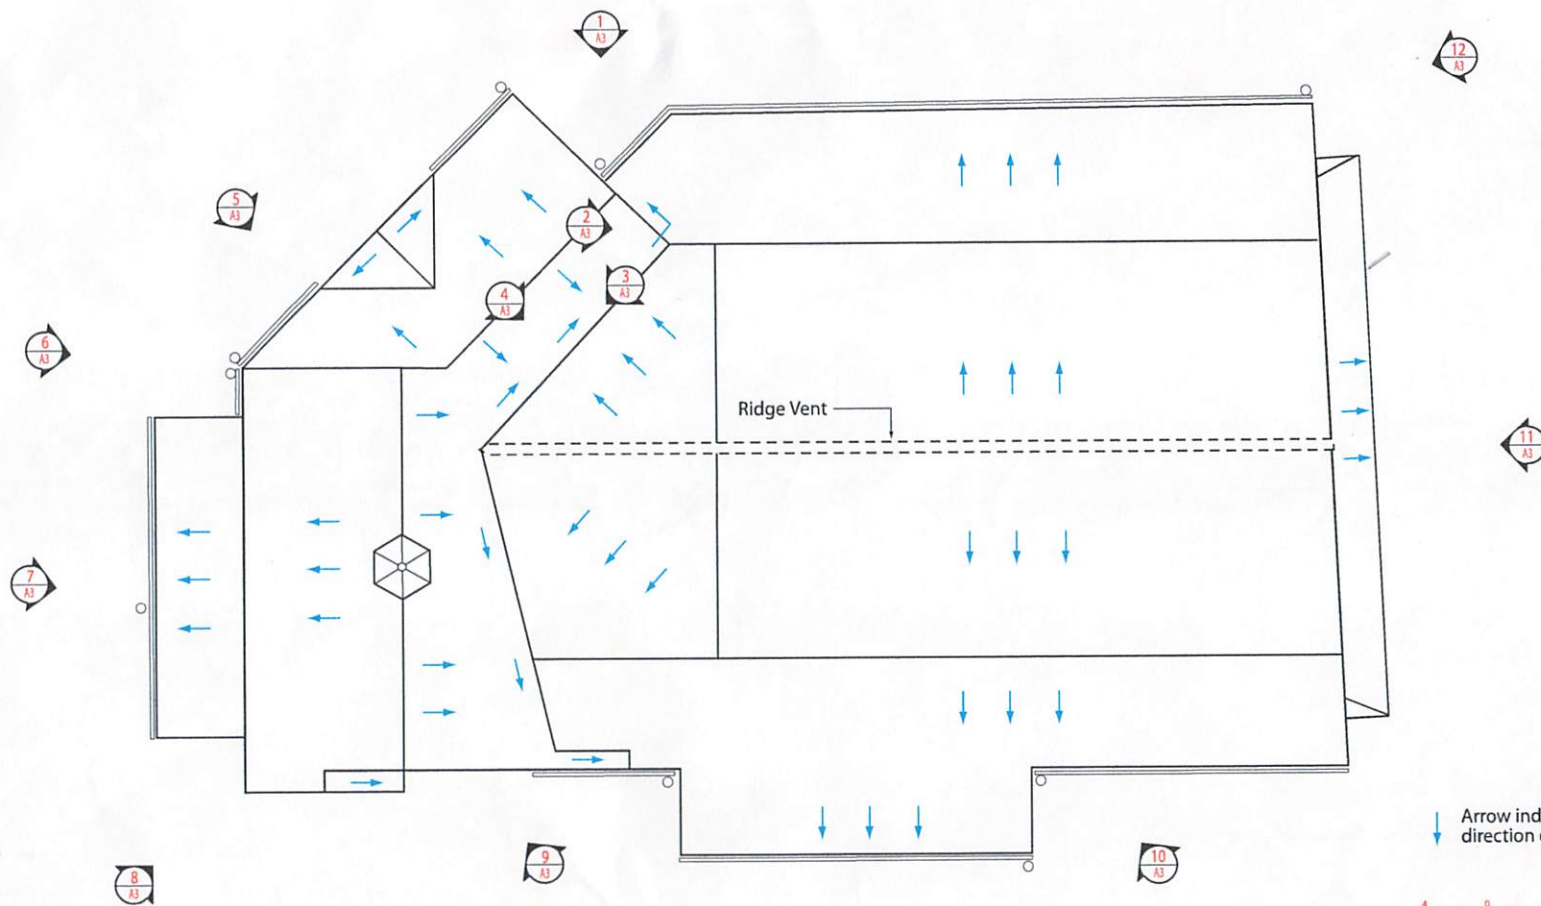

↓ Arrow indicates direction of run-off



DRAWN TRB CHECKED TRB TITLE EXISTING DATE 2006 APR	SHEET NO. TOTAL SHEETS A2	TITLE OF SHEET EXISTING CONDITIONS AND ROOF DRAINAGE PATTERN POINT PARK VISITOR CENTER CHICKAMAUGA AND CHATTANOOGA NATIONAL MILITARY PARK	DRAWING NO. XXXX PROJECT NO. 010000 SHEET NO. X OF XX
---	-------------------------------------	---	--



1 ELEVATION
A3 NOT TO SCALE



2 ELEVATION
A3 NOT TO SCALE



3 ELEVATION
A3 NOT TO SCALE



4 ELEVATION
A3 NOT TO SCALE



5 ELEVATION
A3 NOT TO SCALE



6 ELEVATION
A3 NOT TO SCALE



7 ELEVATION
A3 NOT TO SCALE



8 ELEVATION
A3



9 ELEVATION
A3 NOT TO SCALE



10 ELEVATION
A3 NOT TO SCALE




11 ELEVATION
A3 NOT TO SCALE



12 ELEVATION
A3 NOT TO SCALE

IP ADDRESS TRB	SUBJECT NO. A3	TITLE OF SHEET PHOTOGRAPHS OF EXISTING CONDITIONS POINT PARK VISITOR CENTER	DRAWING NO. XXXX XXXXXX
DATE TRB			
PROJECT NUMBER			
		CHICKAMAUGA AND CHATTANOOGA NATIONAL MILITARY PARK	
SHEET 2006 APR			PER. NO. NAME 111345 X IF NEW

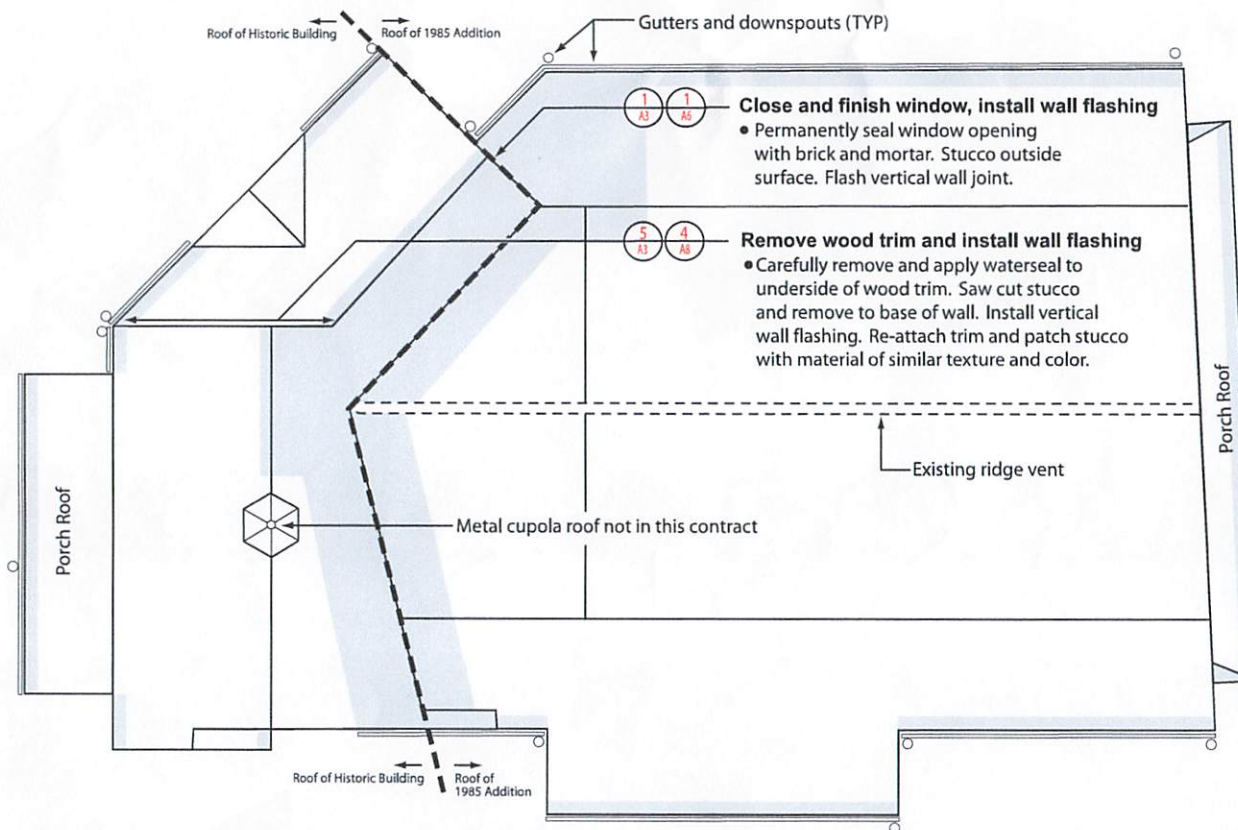

Area of Coverage

Roof Covering Material	Estimated Area of Coverage	Comments
Self-Adhesive Underlayment	4,400 Square Feet	Estimated area includes double layer over area highlighted in gray and 18" at drip edges. See specifications for list of approved manufacturers and products.
Asphalt Shingles	3,750 Square Feet	See specifications for list of approved manufacturers and products.

Note: See Metal Flashing Schedule in Detail 1/A7 for estimate of flashing quantities

GENERAL INSTRUCTIONS

Demolition

- Completely remove and dispose of existing asphalt roof covering and associated materials from building, porch roofs, and other overhangs

Surface Preparation

- Repair or replace damaged decking
- Secure unsupported decking
- Fill all voids and remove protrusions in deck surface

Metal Flashings

- See Metal Flashing Schedule on sheet A5 for flashing details
- Install metal flashings at all vertical wall joints, non-vented ridges, and valleys

Self-Adhesive Underlayment

- Install self-adhesive underlayment over entire deck surface according to manufacturer's instructions
- Install double layer of self-adhesive underlayment over area highlighted in gray

Gutters and Downspouts

- All existing gutters to remain
- Install drip edges
- Straighten and secure all loose or misaligned gutters to fascia board
- Realign and seal connections between gutters and downspouts

Asphalt Shingles

- Install asphalt shingles over self-adhesive underlayment according to manufacturer's instructions


Attic Interior - Bid Additive

- See sheet A-10

4 0 4 8
SCALE OF FEET



DESIGNED	SUB SHEET NO.	SHEET OF SHEET	DRAWING NO.
TRB		A4	XXXX
DATE			XXXX
2008 APR			
ROOF REPLACEMENT PLAN		CHICKAMAUGA AND CHATTANOOGA	
POINT PARK VISITOR CENTER		NATIONAL MILITARY PARK	
FILED		SHEET	
NO.			
172348		X	
CP			

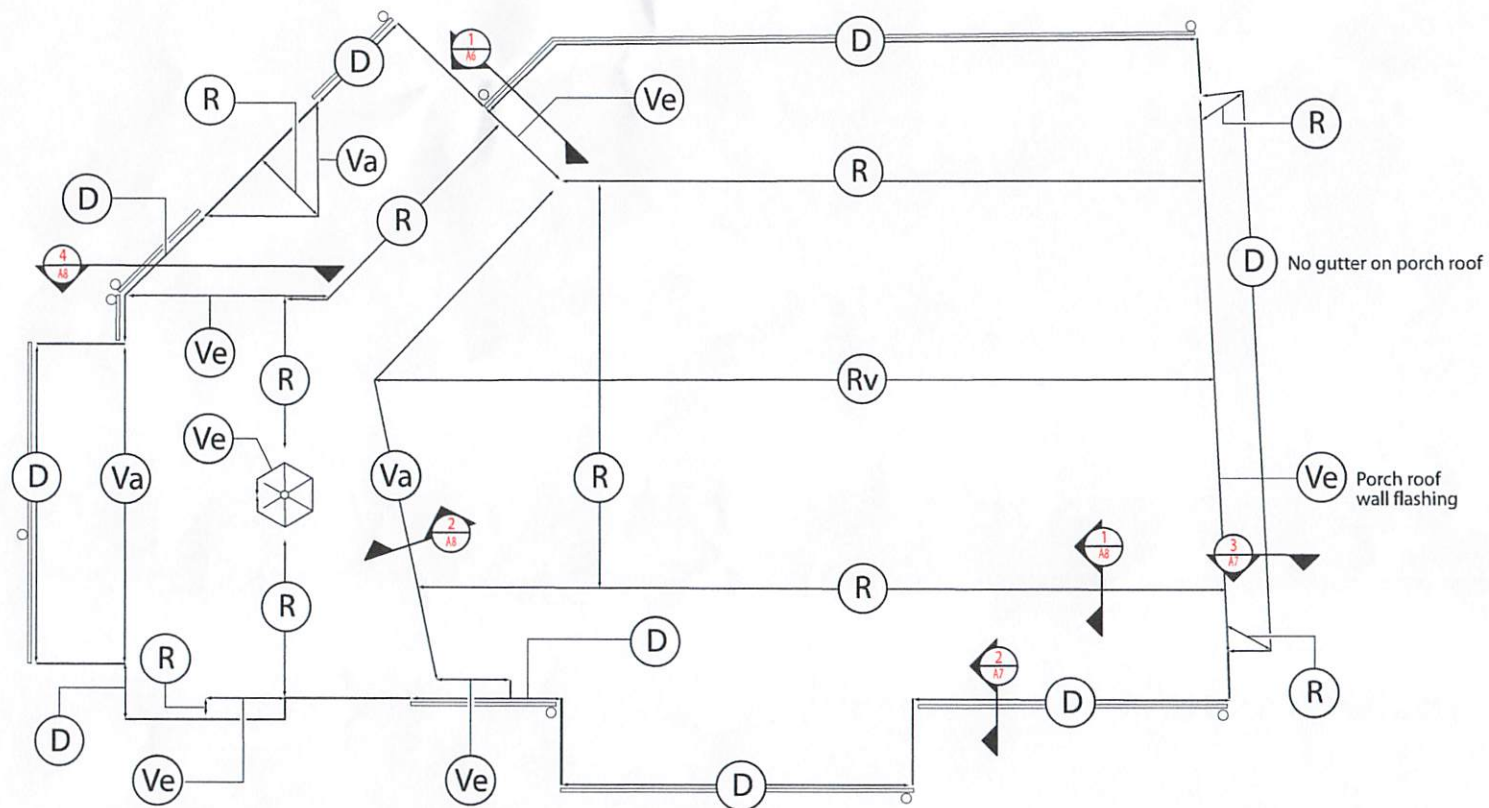


METAL FLASHING SCHEDULE


Symbol	Flashing type	Estimated Quantity	Reference Details	Comments
(D)	Drip Edge	155 LF with gutter 45 LF without gutter	2/A7, 3/A7, 3/A8	See specifications for acceptable materials
(R)	Ridge	180 LF	1/A8	See specifications for acceptable materials
(Rv)	Ridge Vent	Existing	None	Existing vent to be re-used after underlayment is installed
(Va)	Valley	80 LF	2/A8	See specifications for acceptable materials
(Ve)	Vertical Wall Joint	90 LF	2/A6, 1/A7, 1/A9, 2/A9	See specifications for acceptable materials

4 0 4 8
SCALE OF FEET


DATE 2006 APR	SUB SHEET NO. A5	TITLE OF SHEET ROOF REPLACEMENT DETAILS METAL FLASHING SCHEDULE POINT PARK VISITOR CENTER CHICKAMAUGA AND CHATTANOOGA NATIONAL MILITARY PARK	DRAWING NO. XXX SHEET X OF XX
------------------	----------------------------	--	--

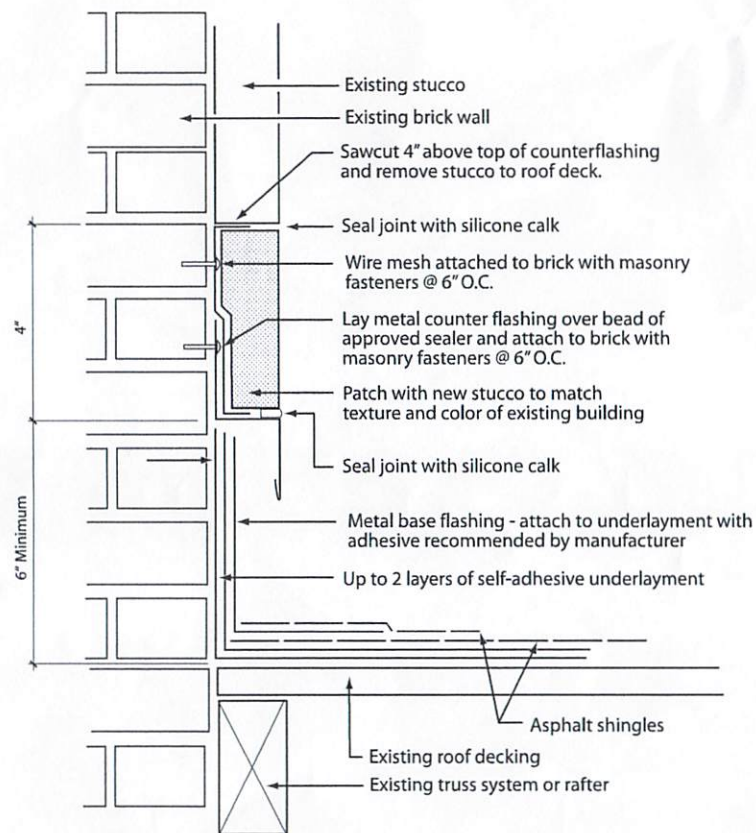

1 Vertical Wall Flashing on Stucco Wall
Not to Scale

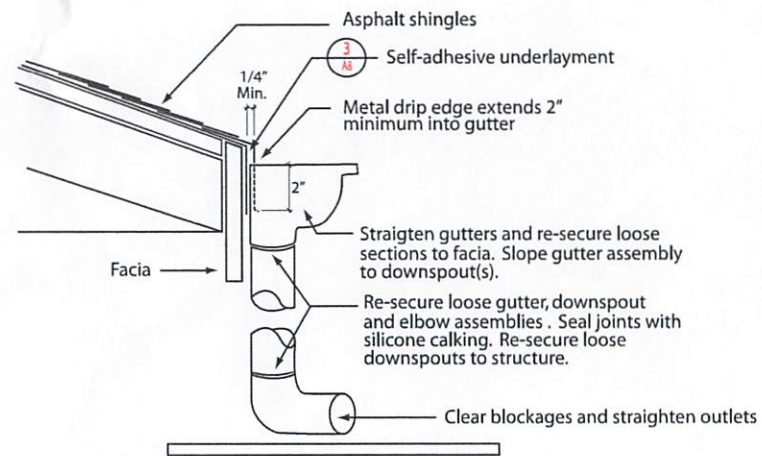


2 Drip Edge with Gutter Detail
Not to Scale

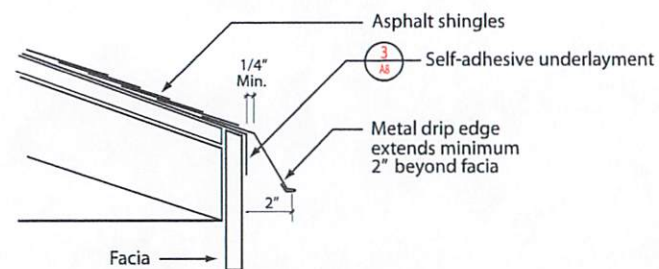


3 Drip Edge without Gutter Detail
Not to Scale


DESIGNED BY		SUB SHEET NO.		TITLE OF SHEET		DRAWING NO.	
TRB		A7		ROOF REPLACEMENT DETAILS METAL FLASHING POINT PARK VISITOR CENTER		X	
CHECKED BY		DATE		PROJECT NO.		SHEET	
TRB		2006 APR		1111111		X	
DATE		2006 APR		1111111		X	
2006 APR		1111111		1111111		X	

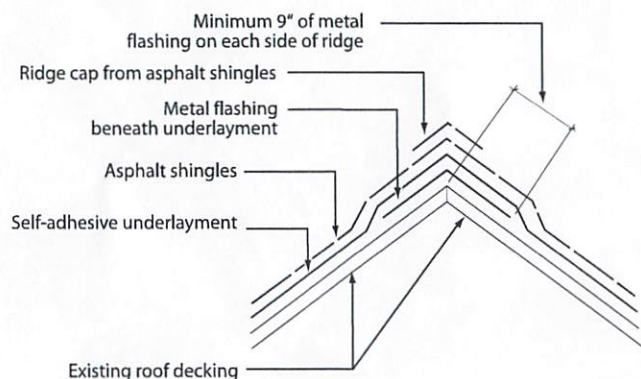


1
A8
Ridge Flashing Detail
Not to Scale

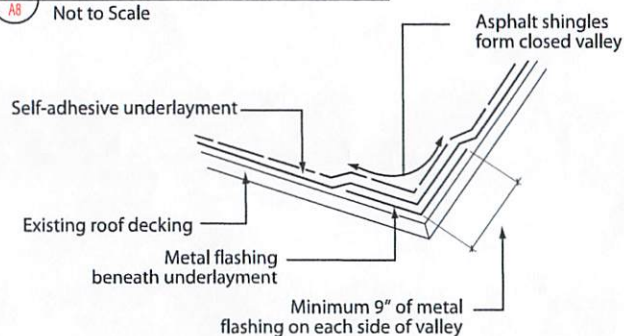

2
A8
Valley Flashing Detail
Not to Scale

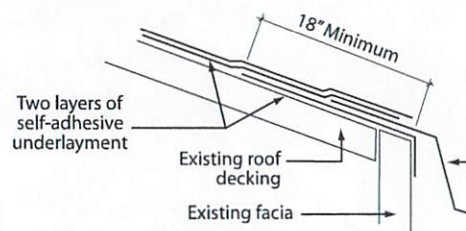

3
A8
Drip Edge and Underlayment Detail
Not to Scale

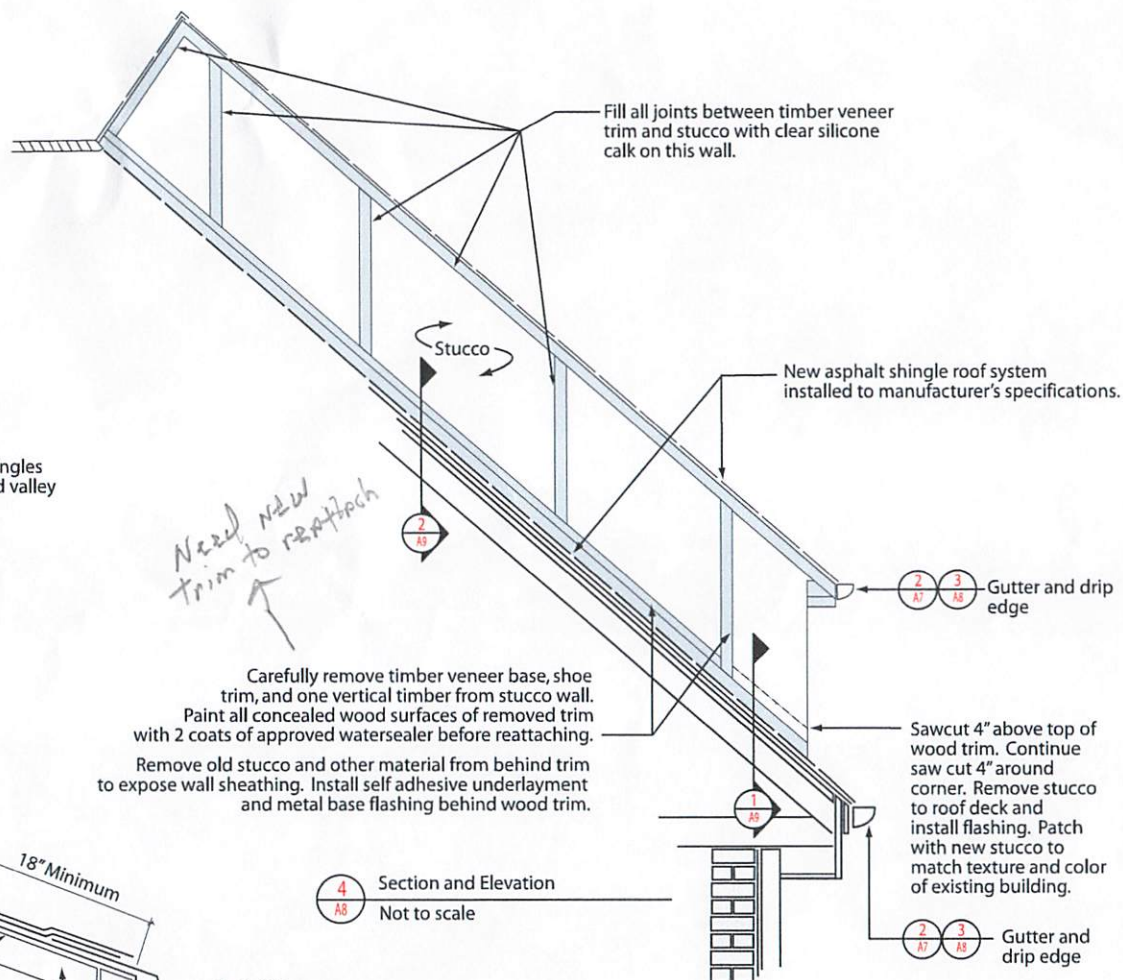

Need new trim to reattach


Carefully remove timber veneer base, shoe trim, and one vertical timber from stucco wall. Paint all concealed wood surfaces of removed trim with 2 coats of approved watersealer before reattaching. Remove old stucco and other material from behind trim to expose wall sheathing. Install self adhesive underlayment and metal base flashing behind wood trim.

4
A8
Section and Elevation
Not to scale


REVISIONS	SUB SHEET NO.	TITLE OF SHEET	DESIGNED BY
TRB		A8	TRB
DATE			SCALE
2006 APR			1/8" = 1'-0"

ROOF REPLACEMENT DETAILS
METAL FLASHING
POINT PARK VISITOR CENTER
CHICKAMAUGA AND CHATTANOOGA
NATIONAL MILITARY PARK

FILE NO.	SHEET
111245	X
OF	XX

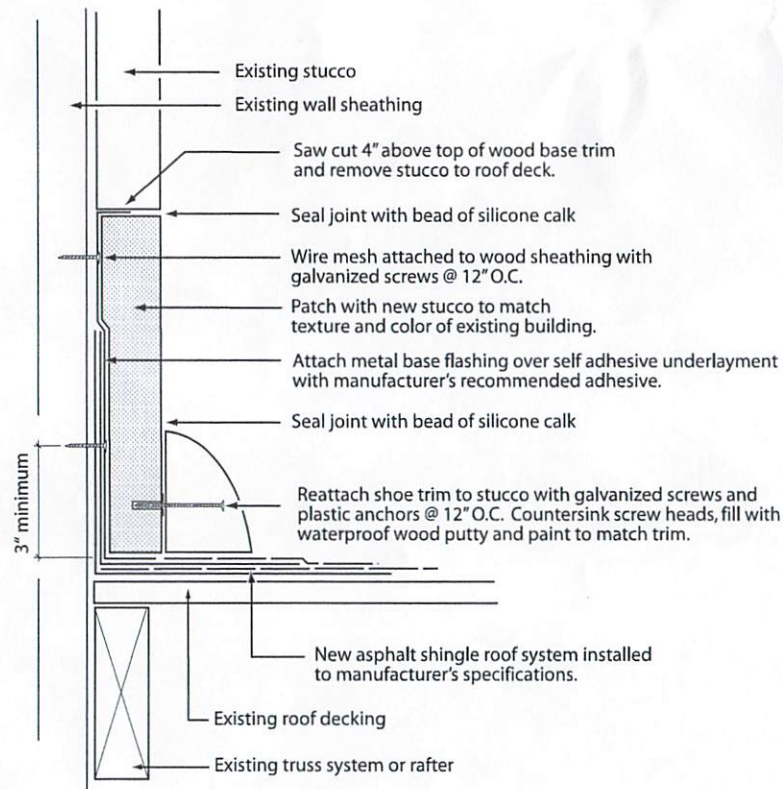


1 Vertical Wall Flashing on Stucco Wall with Wood Shoe Trim
A9 Not to Scale

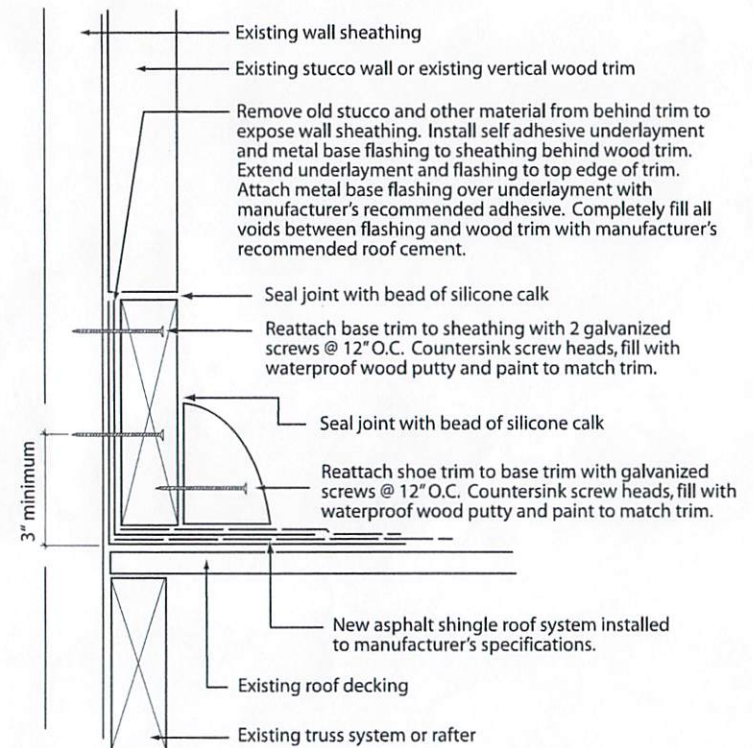

2 Vertical Wall Flashing With Wood Base and Shoe Trim
A9 Not to Scale

DESIGNED	SUB SHEET NO.	TITLE OF SHEET	DRAWN BY
TRB		ROOF REPLACEMENT DETAILS	SCALE
TRB		METAL FLASHING	FILE NO.
TRB		POINT PARK VISITOR CENTER	SHEET
DATE		CHICKAMAUGA AND CHATTAHOOGA	DATE
2006 APR		NATIONAL MILITARY PARK	01/24/06

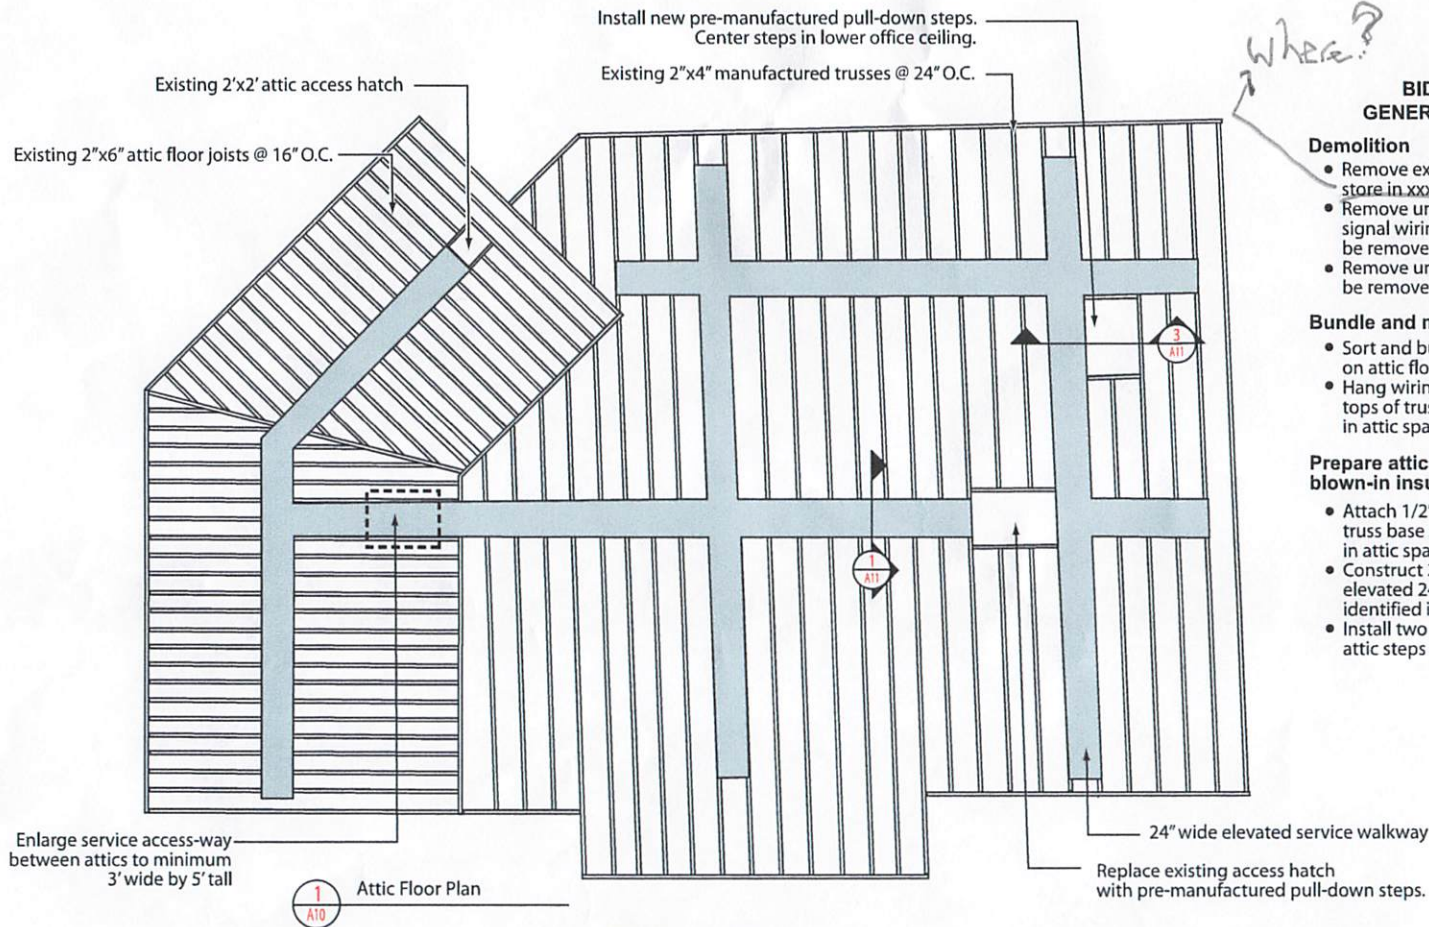

BID ADDITIVE "A" **GENERAL INSTRUCTIONS**

Demolition

- Remove existing batt insulation and store in xxxxxxxx building for future use.
- Remove unused electrical and electronic signal wiring from attic space. Wiring to be removed will be marked by park staff.
- Remove unused HVAC ductwork. Ducts to be removed will be marked by park staff.

Bundle and move loose wiring

- Sort and bundle loose wiring currently on attic floor into harnesses using plastic ties.
- Hang wiring harnesses minimum 24" above tops of truss base supports or ceiling joists in attic spaces.

Prepare attic floors for installation of blown-in insulation



- Attach 1/2" thick plywood sheets to tops of truss base supports and floor joists in attic spaces using 1" wallboard screws
- Construct 24" wide wooden access walkways elevated 24" above attic floor in locations identified in 1/A10.
- Install two sets of pre-manufactured pull-down attic steps in locations identified in 1/A10

Area of Coverage

Item description	Estimated Area of Coverage	Comments
Attic floor - 1/2" plywood	3,400 Square Feet	Interior construction grade plywood. See specifications for list of approved materials.
24" wide wooden service walkway	230 Linear Feet	See details 1/A11, 2/A11, and 3/A11
Pull-down attic steps	Quantity = 2	See specifications for list of approved manufacturers and products.



DESIGNED TRB	SUB SHEET NO. A10	TITLE OF SHEET BID ADDITIVE "A" ATTIC FLOOR AND WALKWAYS POINT PARK VISITOR CENTER	DRAWN/REVIEWED SOURCE
CHECKED TRB			
DATE 2006 APR		CHICKAMAUGA AND CHATTANOOGA NATIONAL MILITARY PARK	SHEET 10 OF 10

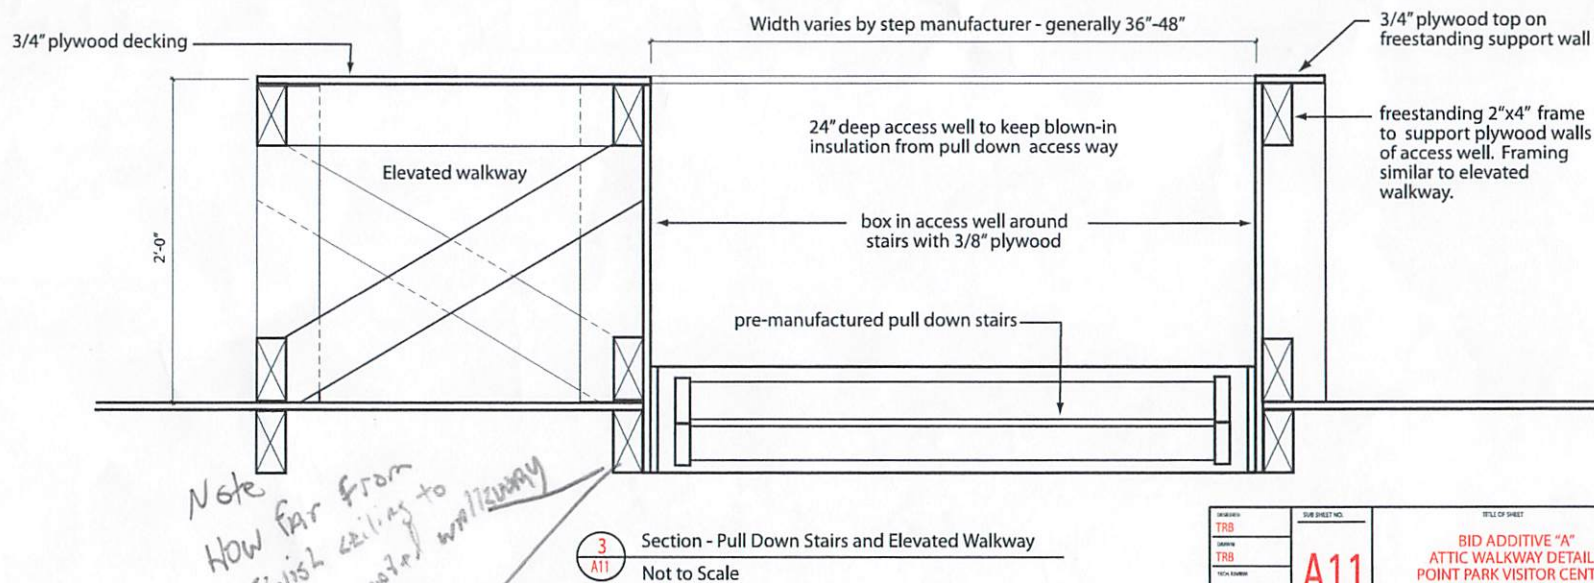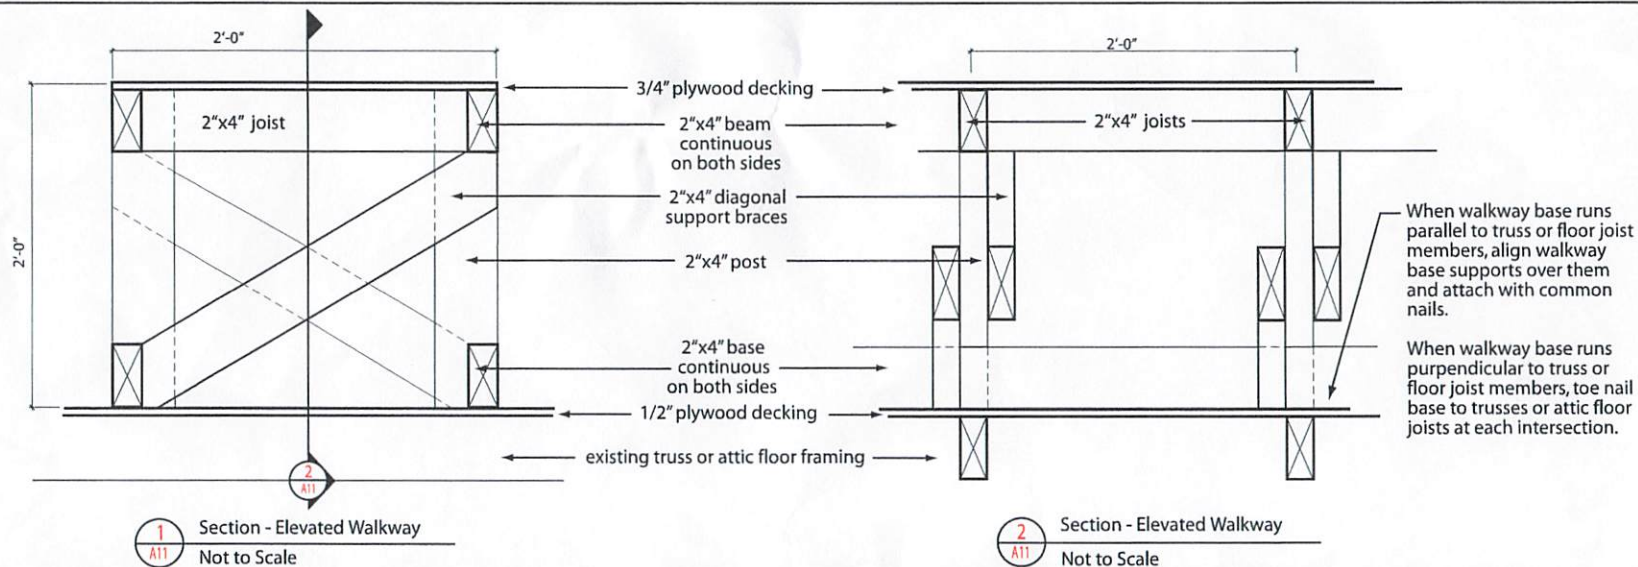

Note how far from finish ceiling to elevated walkway

Is stairs flush with drop ceiling

DESIGNED BY TRB	SUB SHEET NO. A11	TITLE OF SHEET BID ADDITIVE "A" ATTIC WALKWAY DETAILS POINT PARK VISITOR CENTER CHICKAMAUGA AND CHATTANOOGA NATIONAL MILITARY PARK	DATE 2006 APR	DRWING NO. J-001	REV. NO. 1	SHEET X	OF XX
--------------------	-----------------------------	--	------------------	---------------------	---------------	------------	----------


* Closest vehicle access point

1
A13


Note: The Ochs Museum is accessible only by paved foot trail. Due to steep and rocky terrain, motor vehicles are unable to drive closer than 200' to the structure.

2
A13

Paved foot trail and steps

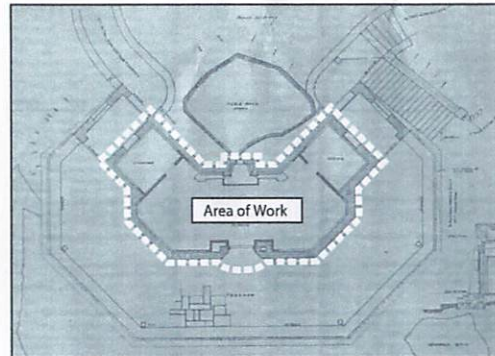

1
A12 ROOF PLAN AND SITE LAYOUT
NOT TO SCALE

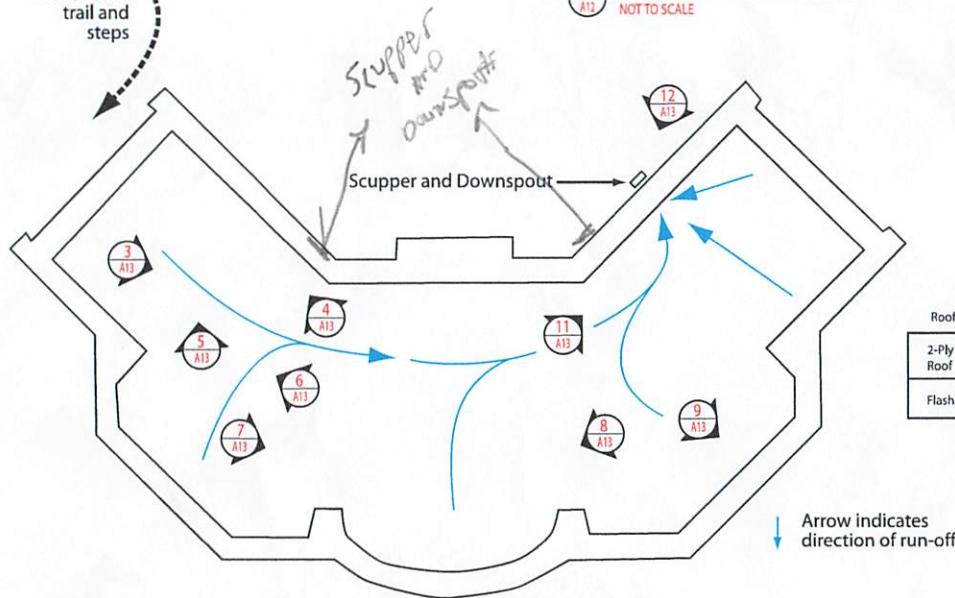

2
A13 EXISTING CONDITIONS
NOT TO SCALE

GENERAL INSTRUCTIONS

Demolition

- Completely remove existing modified bituminous roof covering and associated materials from building
- Dispose of removed materials off site

Surface Preparation

- Allow existing roof deck to dry
- Repair or replace damaged cants
- Fill all voids and remove protrusions in deck surface
- Fill cored holes of missing iron spikes on top of parapet wall with grout

Repoint and Seal Parapet Wall - Bid Additive

- See sheet A14

Install 2-Ply SBS Modified Bituminous Roof System

- Install first ply and flashing as appropriate over entire deck surface according to manufacturer's instructions
- Install waterproof membrane and flashing over first ply according to manufacturer's instructions
- Install counterflashing, see detail 2/A14

Area of Coverage

Roof Covering Material	Estimated Area of Coverage	Comments
2-Ply SBS Modified Butuninus Roofing System	600 Square Feet	Cold or torch applied system. See specifications for list of approved manufacturers and products.
Flashing and counterflashing	850 Linear Feet	See specifications for list of approved manufacturers and products.

Arrow indicates direction of run-off

DATE 2006 APR	SUB SHEET NO. A12	TITLE OF SHEET EXISTING CONDITIONS AND ROOF REPLACEMENT PLAN OCHS MUSEUM BUILDING CHICKAMAUGA AND CHATTANOOGA NATIONAL MILITARY PARK	DRAWING NO. XXXX
DESIGNED TRB	CHECKED TRB	DATE 01/24/06	SHEET X



1
A13 ELEVATION
NOT TO SCALE



2
A13 ELEVATION
NOT TO SCALE



3
A13 ELEVATION
NOT TO SCALE



4
A13 ELEVATION
NOT TO SCALE



5
A13 ELEVATION
NOT TO SCALE



6
A13 ELEVATION
NOT TO SCALE



7
A13 ELEVATION
NOT TO SCALE



8
A13 ELEVATION
NOT TO SCALE



9
A13 ELEVATION
NOT TO SCALE



10
A13 ELEVATION
NOT TO SCALE




11
A13 ELEVATION
NOT TO SCALE




12
A13 ELEVATION
NOT TO SCALE


DESIGNED TRB	SUB SHEET NO. A13	TITLE OF SHEET PHOTOGRAPHS OF EXISTING CONDITIONS OCHS MUSEUM BUILDING CHICKAMAUGA AND CHATTANOOGA NATIONAL MILITARY PARK	DATE 2006 APR	PROJECT NO. 012140	SHEET X
-----------------	-----------------------------	---	------------------	-----------------------	------------

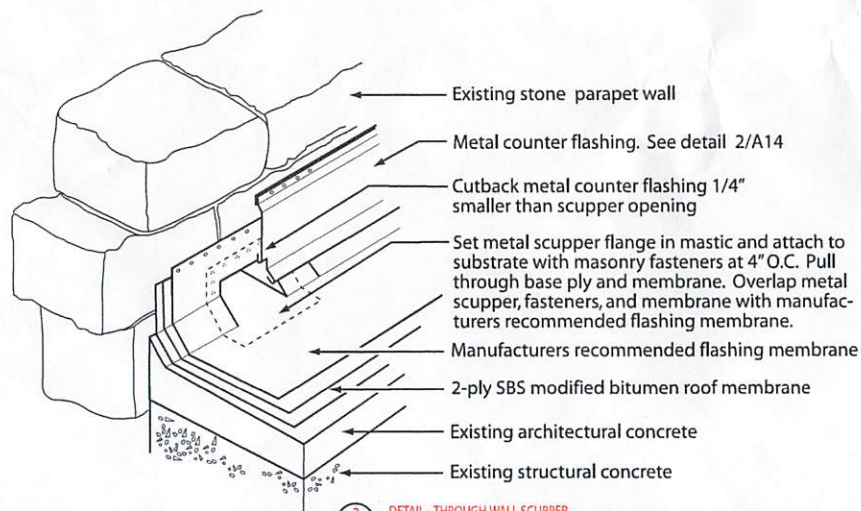

3 DETAIL - THROUGH WALL SCUPPER
A14
NOT TO SCALE

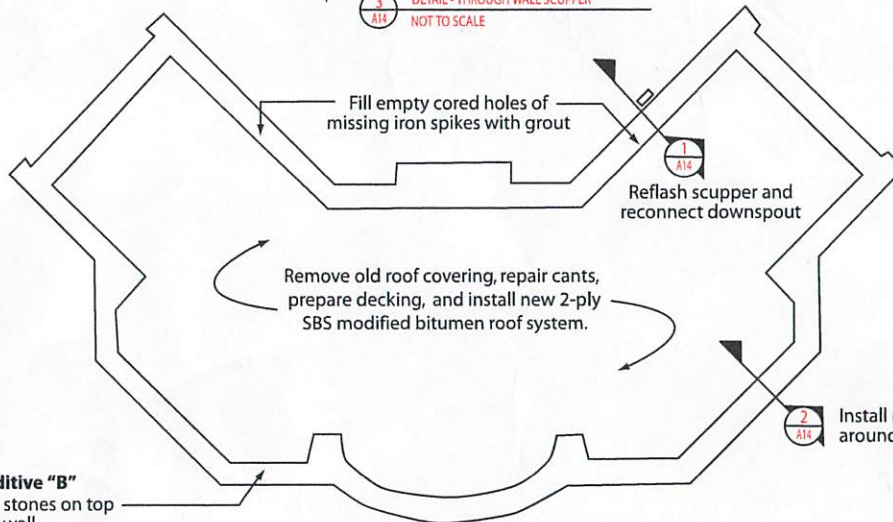

1 ROOF IMPROVEMENTS
14
NOT TO SCALE

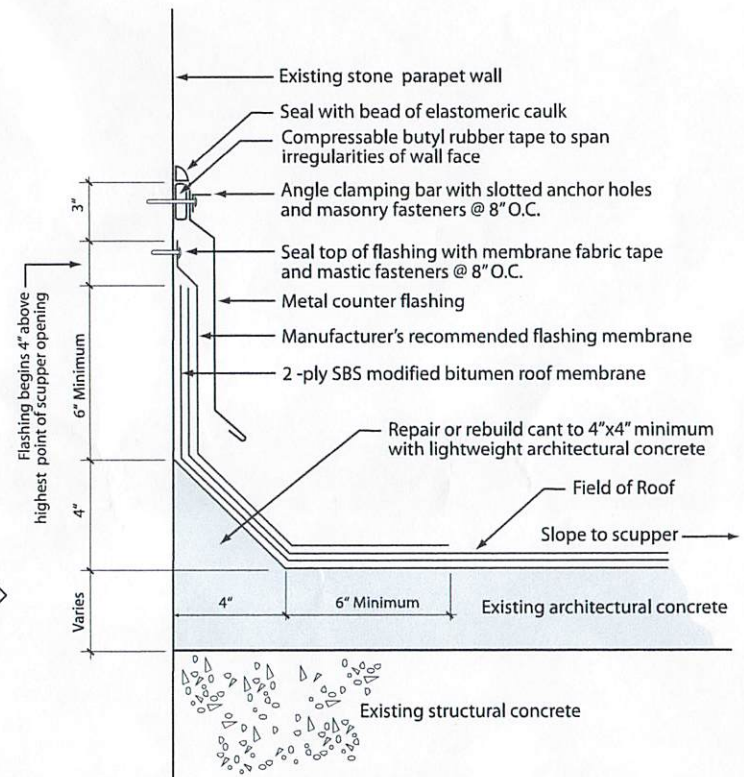

2 SECTION - FLASHING, CANT, AND COUNTER FLASHING
A14
NOT TO SCALE

2 A14
Install new counterflashing around interior of parapet wall

DESIGNED TRB	SUB SHEET NO. A14	TITLE OF SHEET FLASHING DETAILS AND BID ADDITIVE "B" OCHS MUSEUM BUILDING CHICKAMAUGA AND CHATTANOOGA NATIONAL MILITARY PARK	DRAWING NO. XXXX
APPROVED TRB			DATE 01/23/06
DATE 2006 APR			SHEET X