


WWYK170123

REPAIR ROOF, LOG FCLTY


DEP OPS B201

KEY PLAN:

A key plan map showing a building layout. The map is divided into a grid with letters A, B, C, D, E on the left and numbers 1, 2 on the top and bottom. Building 201 is highlighted in red. Other buildings are labeled with numbers: 215, 272, 284, 285, 296, 202, 246, 229, 233, and 283. A line points from the text 'PROJECT LOCATION' to building 201. A north arrow is in the bottom right corner.

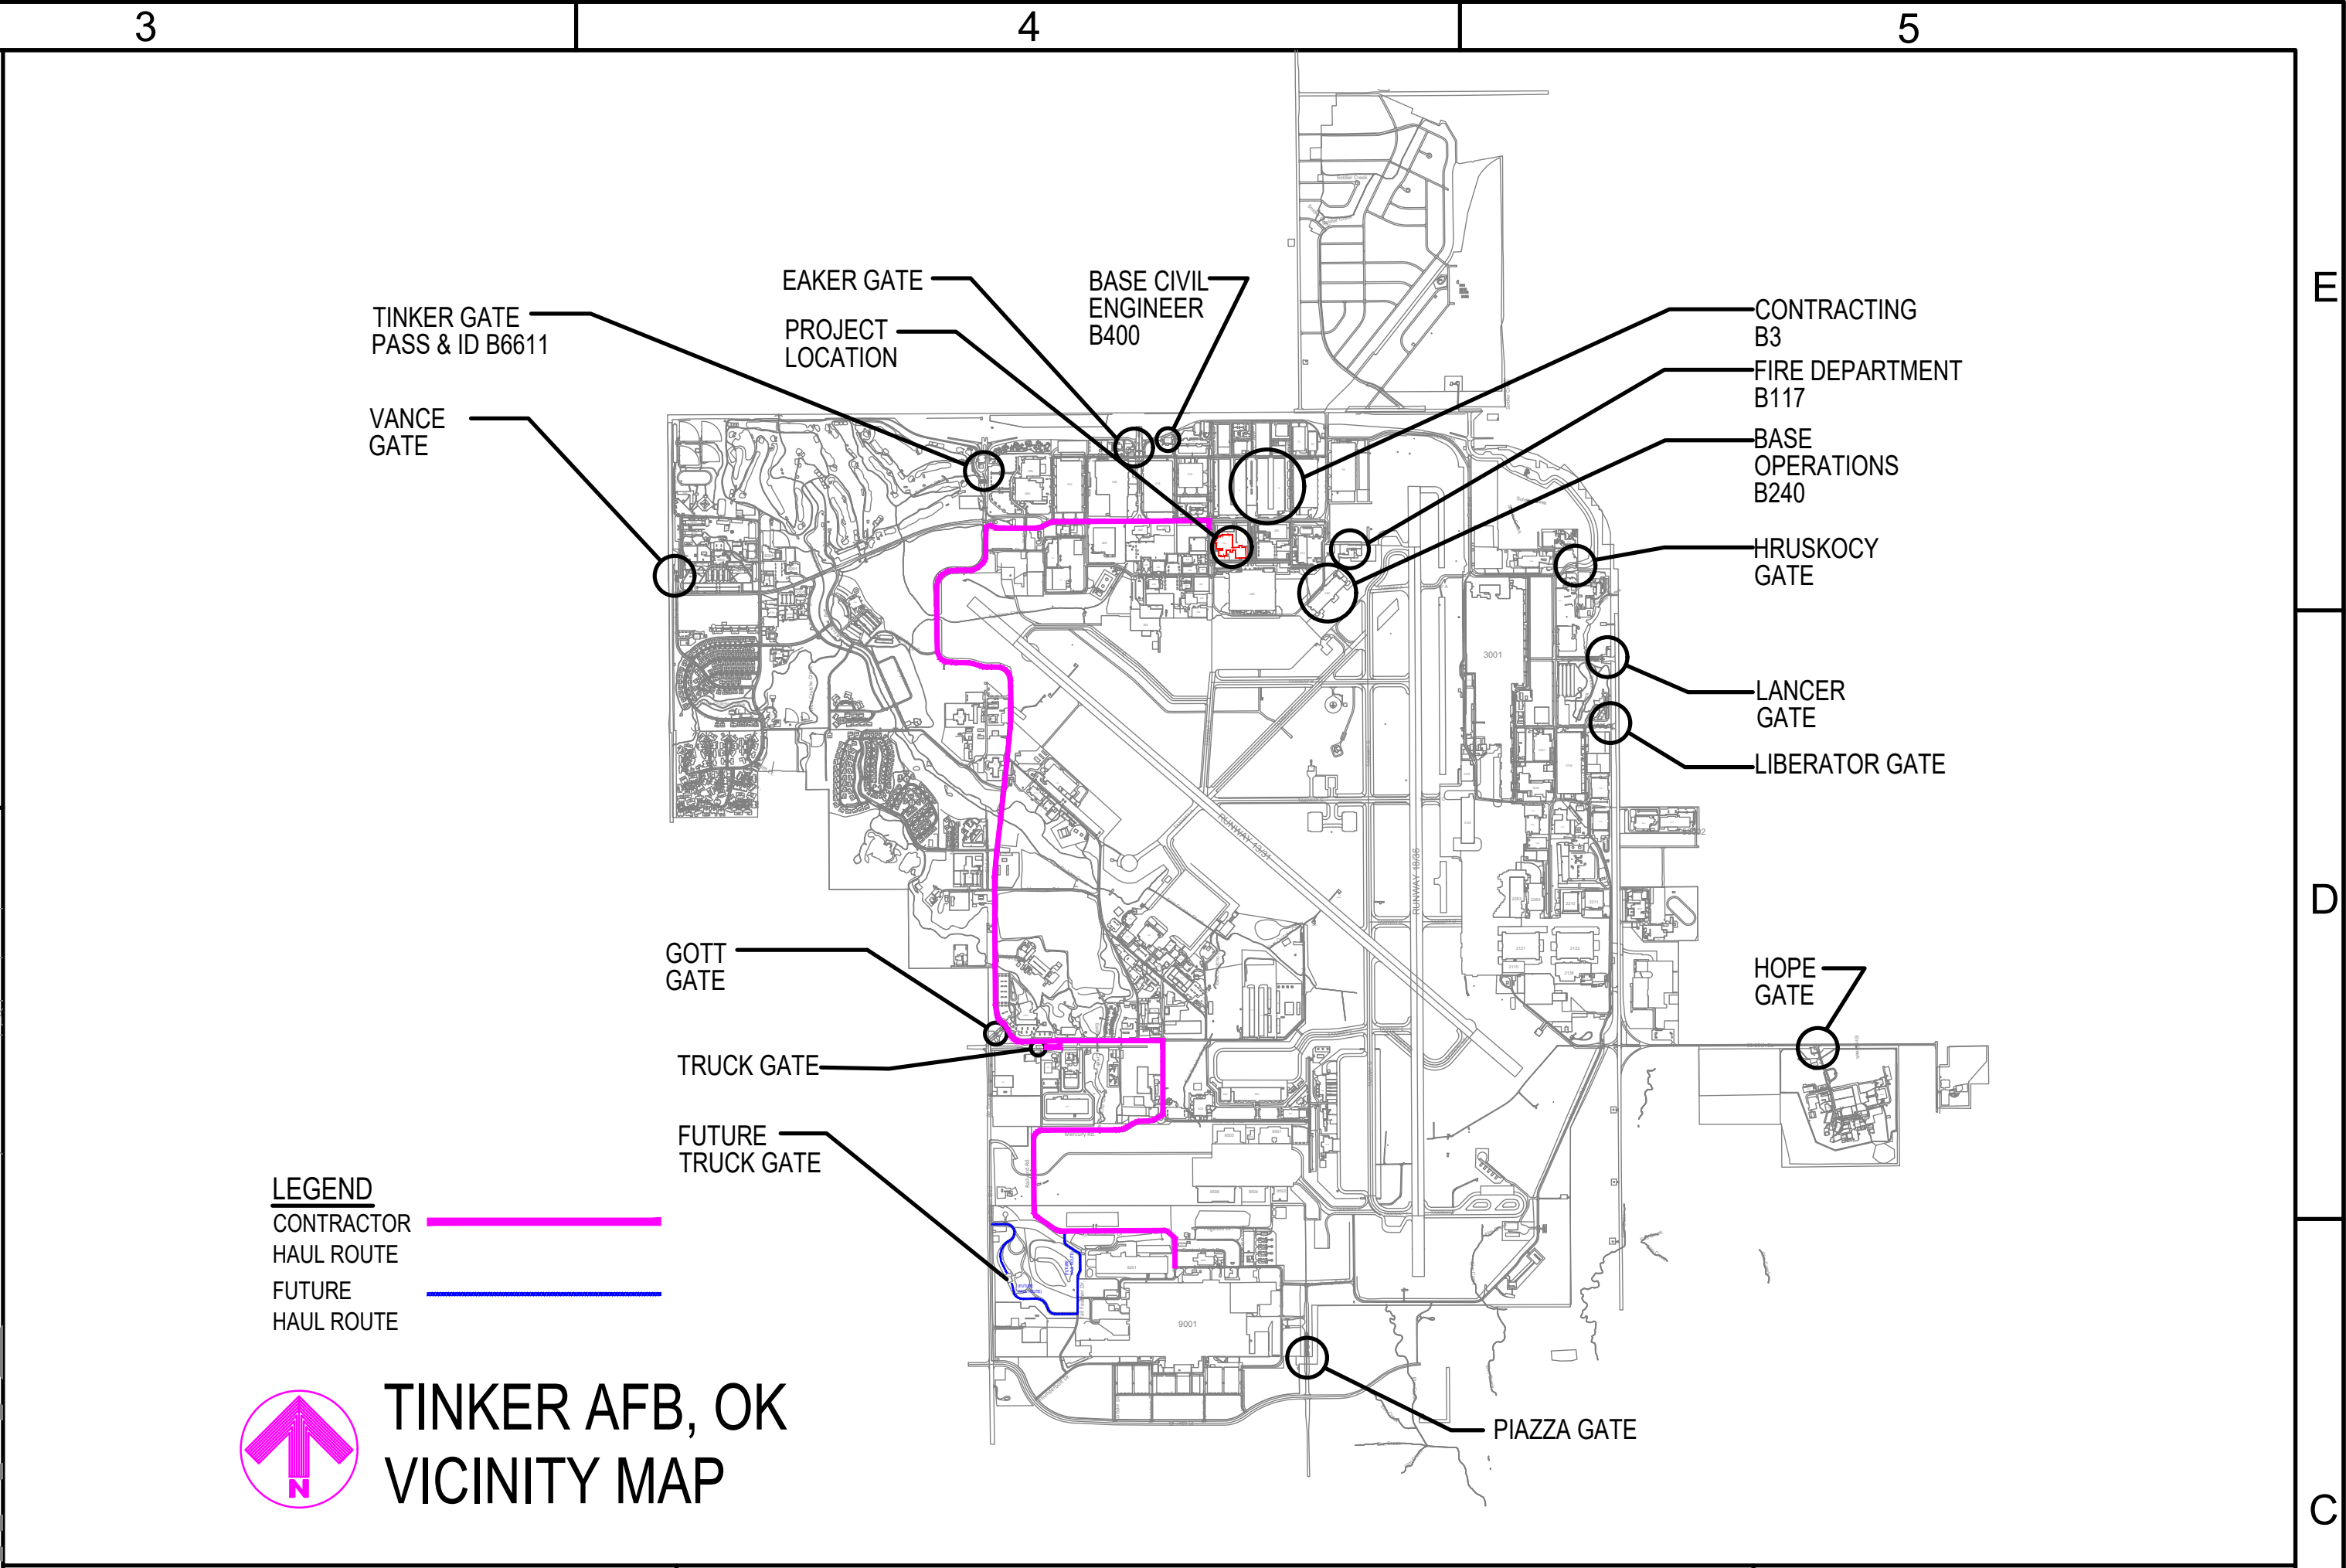

 AIR FORCE MATERIEL COMMAND 72 ABW CIVIL ENGINEER DIRECTORATE TINKER AFB, OK																													
35 % DESIGN																													
WWWY170123 REPAIR ROOF, LOG FCLTY DEP OPS B201																													
PROJECT INFORMATION: TINKER AIR FORCE BASE, OKLAHOMA																													
MANAGEMENT INFORMATION: <table border="1" style="width: 100%; border-collapse: collapse;"> <thead> <tr> <th style="width: 60%; padding: 5px;">REVISIONS</th> <th style="width: 40%; padding: 5px;">MARK</th> <th style="width: 40%; padding: 5px;">DATE</th> <th style="width: 60%; padding: 5px;">DESCRIPTION</th> </tr> </thead> <tbody> <tr> <td style="padding: 5px;">ISSUE DATE: 8 APRIL 2026</td> <td></td> <td></td> <td></td> </tr> <tr> <td style="padding: 5px;">DESIGN GROUP: THDR-SRM</td> <td></td> <td></td> <td></td> </tr> <tr> <td style="padding: 5px;">DESIGNED BY:</td> <td></td> <td></td> <td></td> </tr> <tr> <td style="padding: 5px;">DRAWN BY: P GOUCHER</td> <td></td> <td></td> <td></td> </tr> <tr> <td style="padding: 5px;">CHECKED BY: S SWIFT</td> <td></td> <td></td> <td></td> </tr> <tr> <td colspan="4" style="padding: 5px;">DESIGN FILE LOCATION: Engr\Design\2010s\2017\201701230_3_Drawings\Model</td> </tr> </tbody> </table>	REVISIONS	MARK	DATE	DESCRIPTION	ISSUE DATE: 8 APRIL 2026				DESIGN GROUP: THDR-SRM				DESIGNED BY:				DRAWN BY: P GOUCHER				CHECKED BY: S SWIFT				DESIGN FILE LOCATION: Engr\Design\2010s\2017\201701230_3_Drawings\Model				SHEET TITLE: GENERAL NOTES AND VICINITY MAP SHEET NUMBER: G-101 SHEET OF 01 06
REVISIONS	MARK	DATE	DESCRIPTION																										
ISSUE DATE: 8 APRIL 2026																													
DESIGN GROUP: THDR-SRM																													
DESIGNED BY:																													
DRAWN BY: P GOUCHER																													
CHECKED BY: S SWIFT																													
DESIGN FILE LOCATION: Engr\Design\2010s\2017\201701230_3_Drawings\Model																													

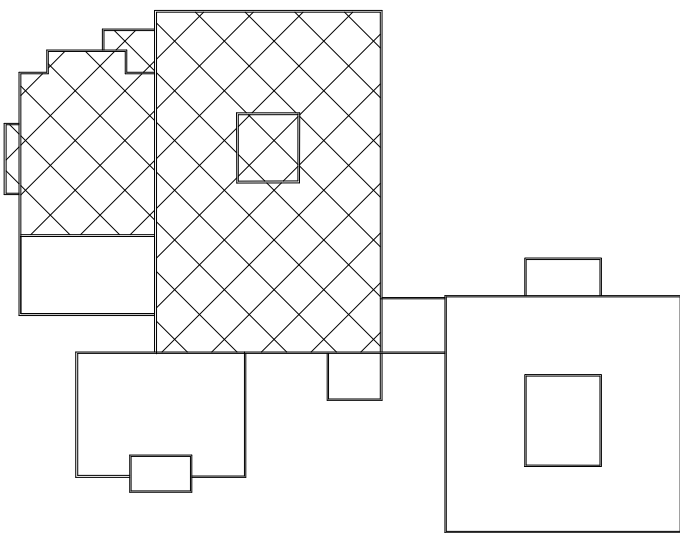


B201 KEY PLAN

35 %
DESIGN


PROJECT INFORMATION
WWYK170123
REPAIR ROOF, LOG FCULTY
DEP OPS B201
TINKER AIR FORCE BASE, OKLAHOMA

MANAGEMENT INFORMATION		REVISIONS	
ISSUE DATE	8 APRIL 2026	MARK	DATE DESCRIPTION
DESIGN GROUP	THDR-SRM		
DESIGNED BY	A ALAWADI		
DRAWN BY	P GOUCHER		
CHECKED BY	S SWIFT		
DESIGN FILE LOCATION	Engr\Design\2017052017201701230_Support\0_3_Drawings\Model		

SHEET TITLE
AERIAL IMAGE
OF B201 ROOF

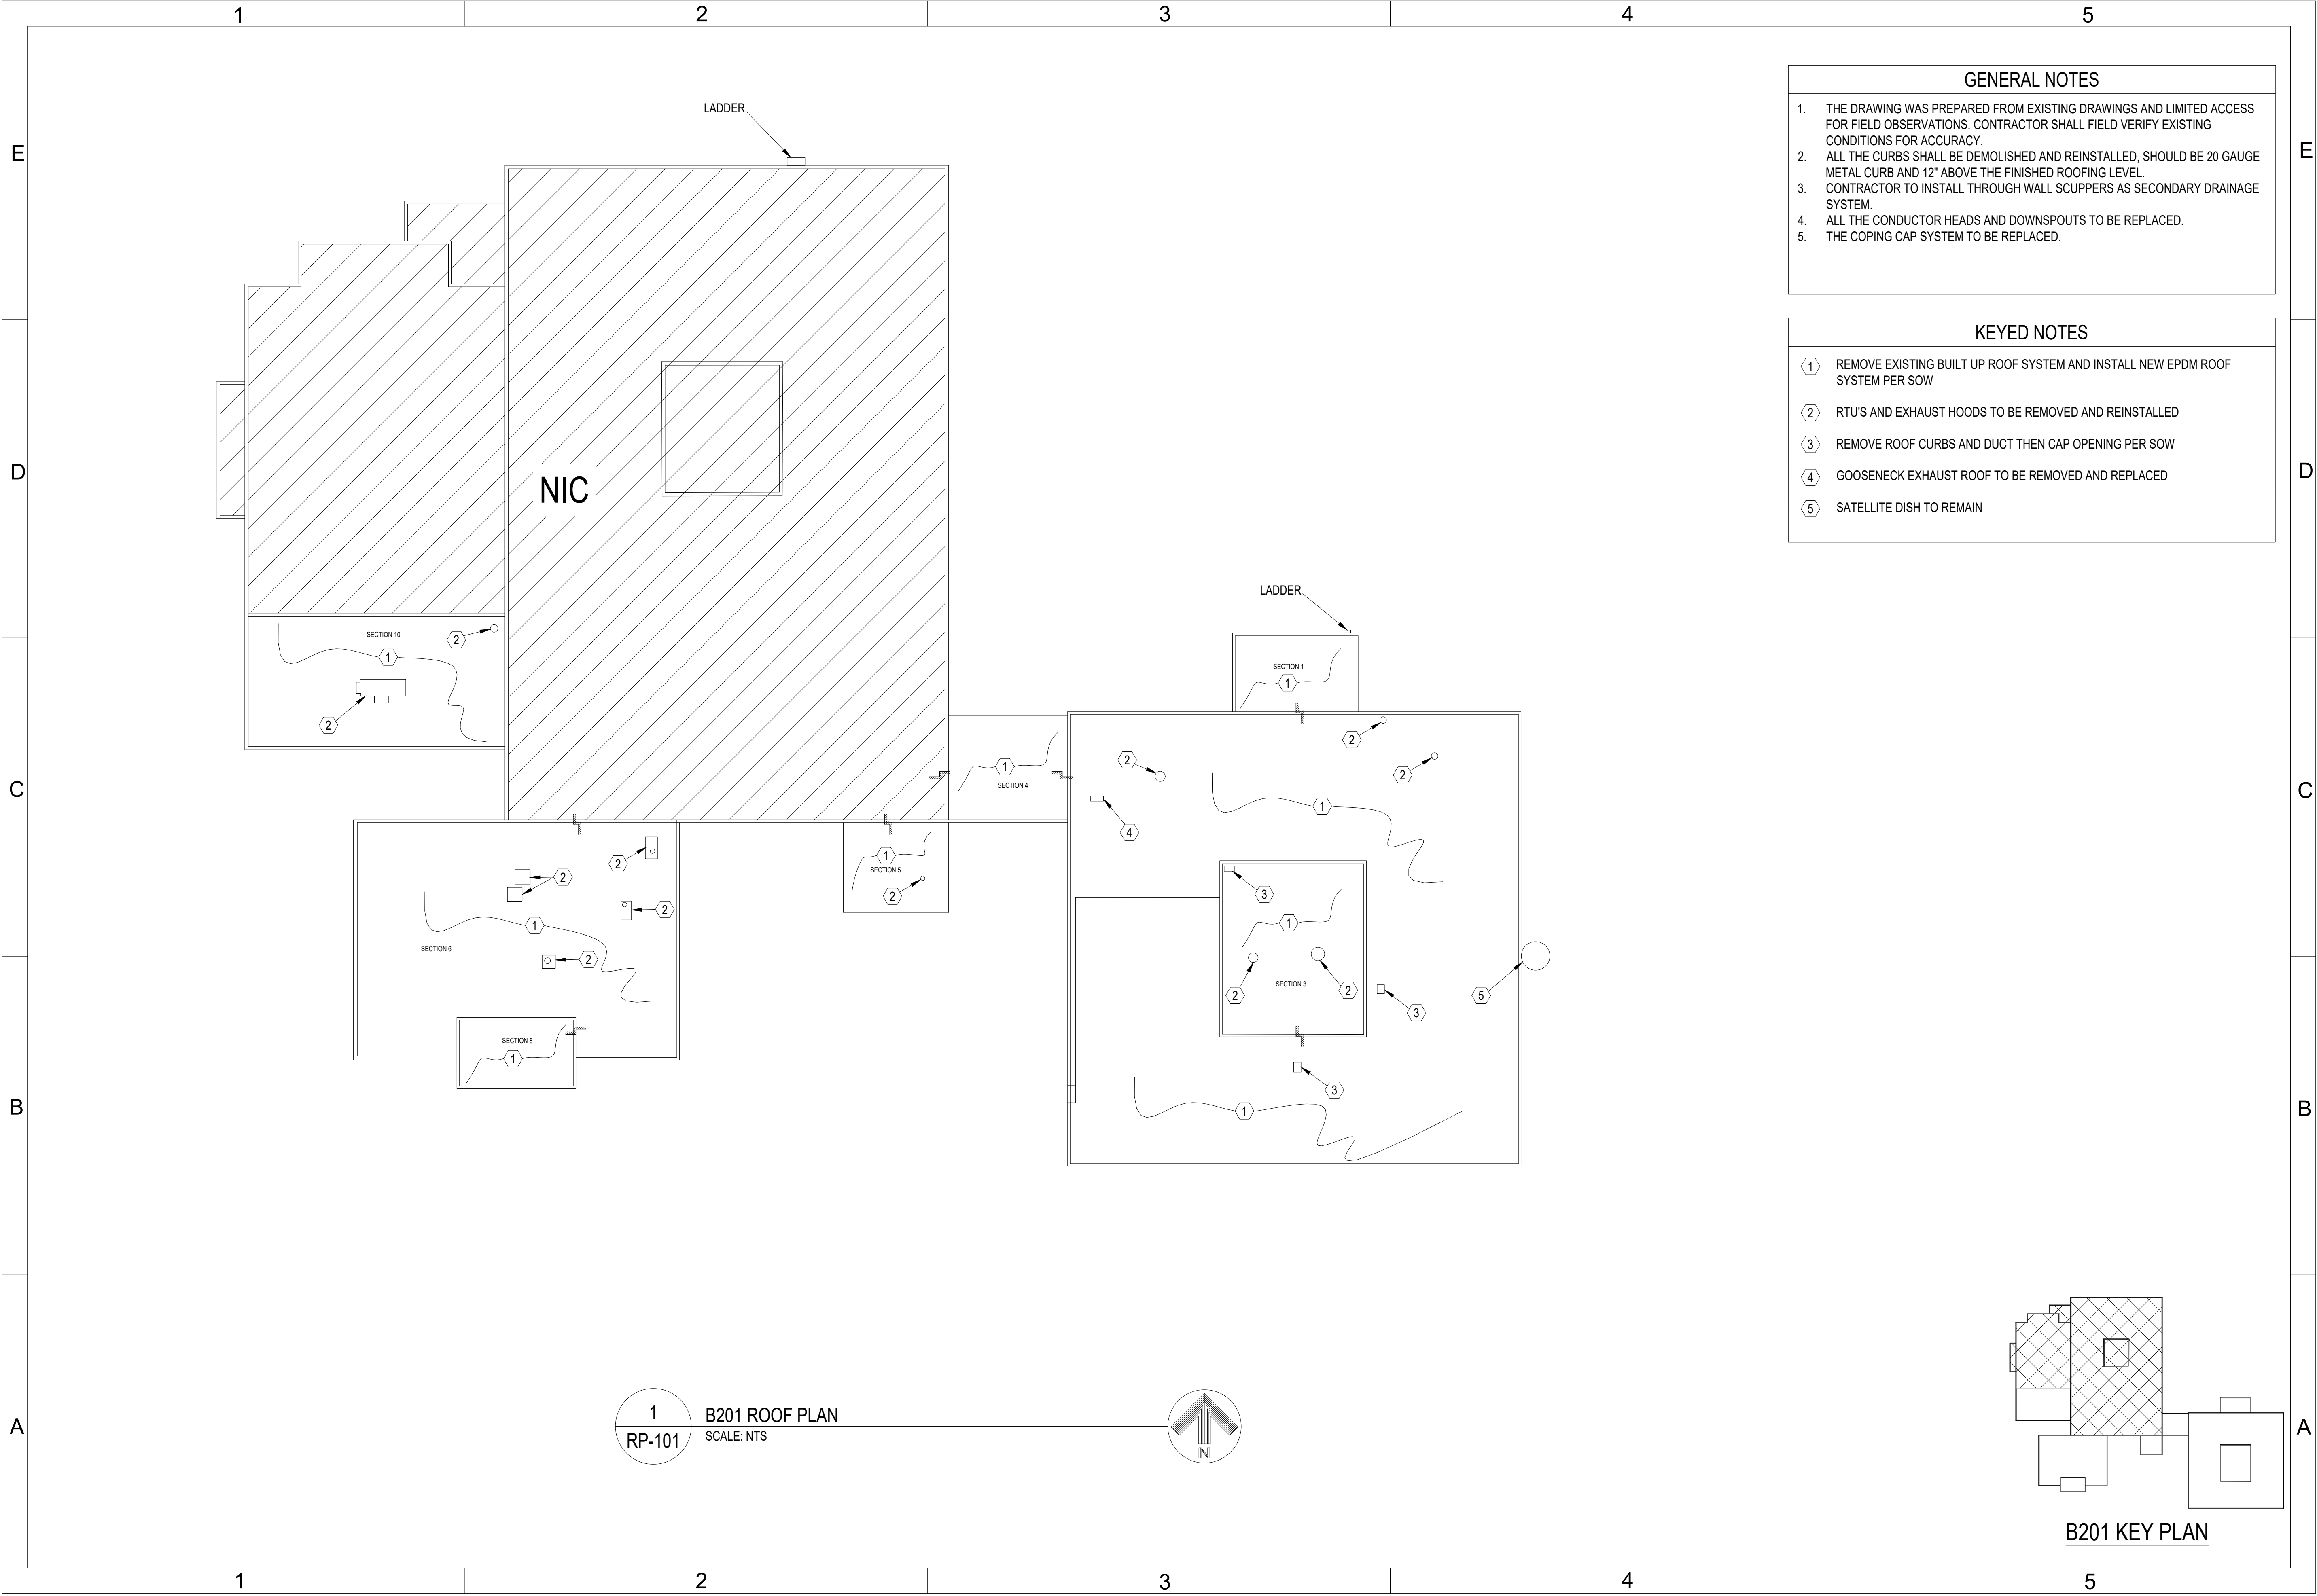

1
RP-101
B201 ROOF PLAN
SCALE: NTS

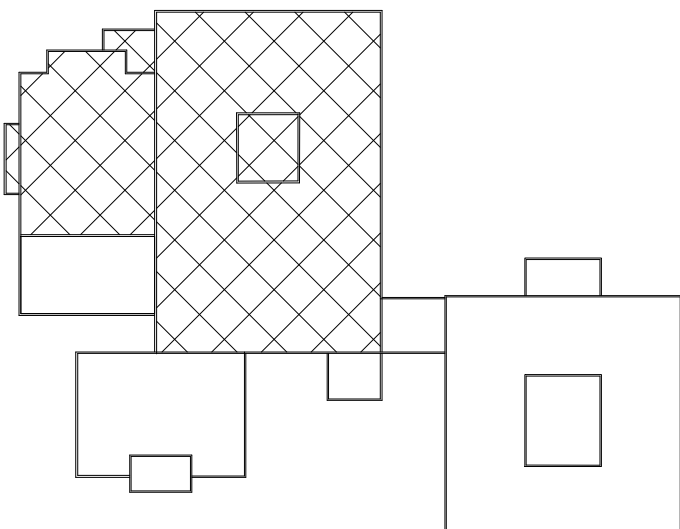

B201 KEY PLAN

GENERAL NOTES

1. THE DRAWING WAS PREPARED FROM EXISTING DRAWINGS AND LIMITED ACCESS FOR FIELD OBSERVATIONS. CONTRACTOR SHALL FIELD VERIFY EXISTING CONDITIONS FOR ACCURACY.
2. ALL THE CURBS SHALL BE DEMOLISHED AND REINSTALLED, SHOULD BE 20 GAUGE METAL CURB AND 12" ABOVE THE FINISHED ROOFING LEVEL.
3. CONTRACTOR TO INSTALL THROUGH WALL SCUPPERS AS SECONDARY DRAINAGE SYSTEM.
4. ALL THE CONDUCTOR HEADS AND DOWNSPOUTS TO BE REPLACED.
5. THE COPING CAP SYSTEM TO BE REPLACED.

KEYED NOTES

- 1 REMOVE EXISTING BUILT UP ROOF SYSTEM AND INSTALL NEW EPDM ROOF SYSTEM PER SOW
- 2 RTU'S AND EXHAUST HOODS TO BE REMOVED AND REINSTALLED
- 3 REMOVE ROOF CURBS AND DUCT THEN CAP OPENING PER SOW
- 4 GOOSENECK EXHAUST ROOF TO BE REMOVED AND REPLACED
- 5 SATELLITE DISH TO REMAIN




35 %
DESIGN

PROJECT INFORMATION
WYK170123
REPAIR ROOF, LOG FCLTY
DEP OPS B201
TINKER AIR FORCE BASE, OKLAHOMA

MANAGEMENT INFORMATION		REVISIONS	
ISSUE DATE	8 APRIL 2026	MARK	DATE DESCRIPTION
DESIGN GROUP	THDR-SRM		
DESIGNED BY	A ALAWADI		
DRAWN BY	P GOUCHER		
CHECKED BY	S SWIFT		
DESIGN FILE LOCATION	Engr\Design\2017\05\2017\20170123\0_Support\0_3_Drawings\Model		

SHEET TITLE
B201 ROOF PLAN

SHEET NUMBER
RP-101
SHEET 03 OF 06

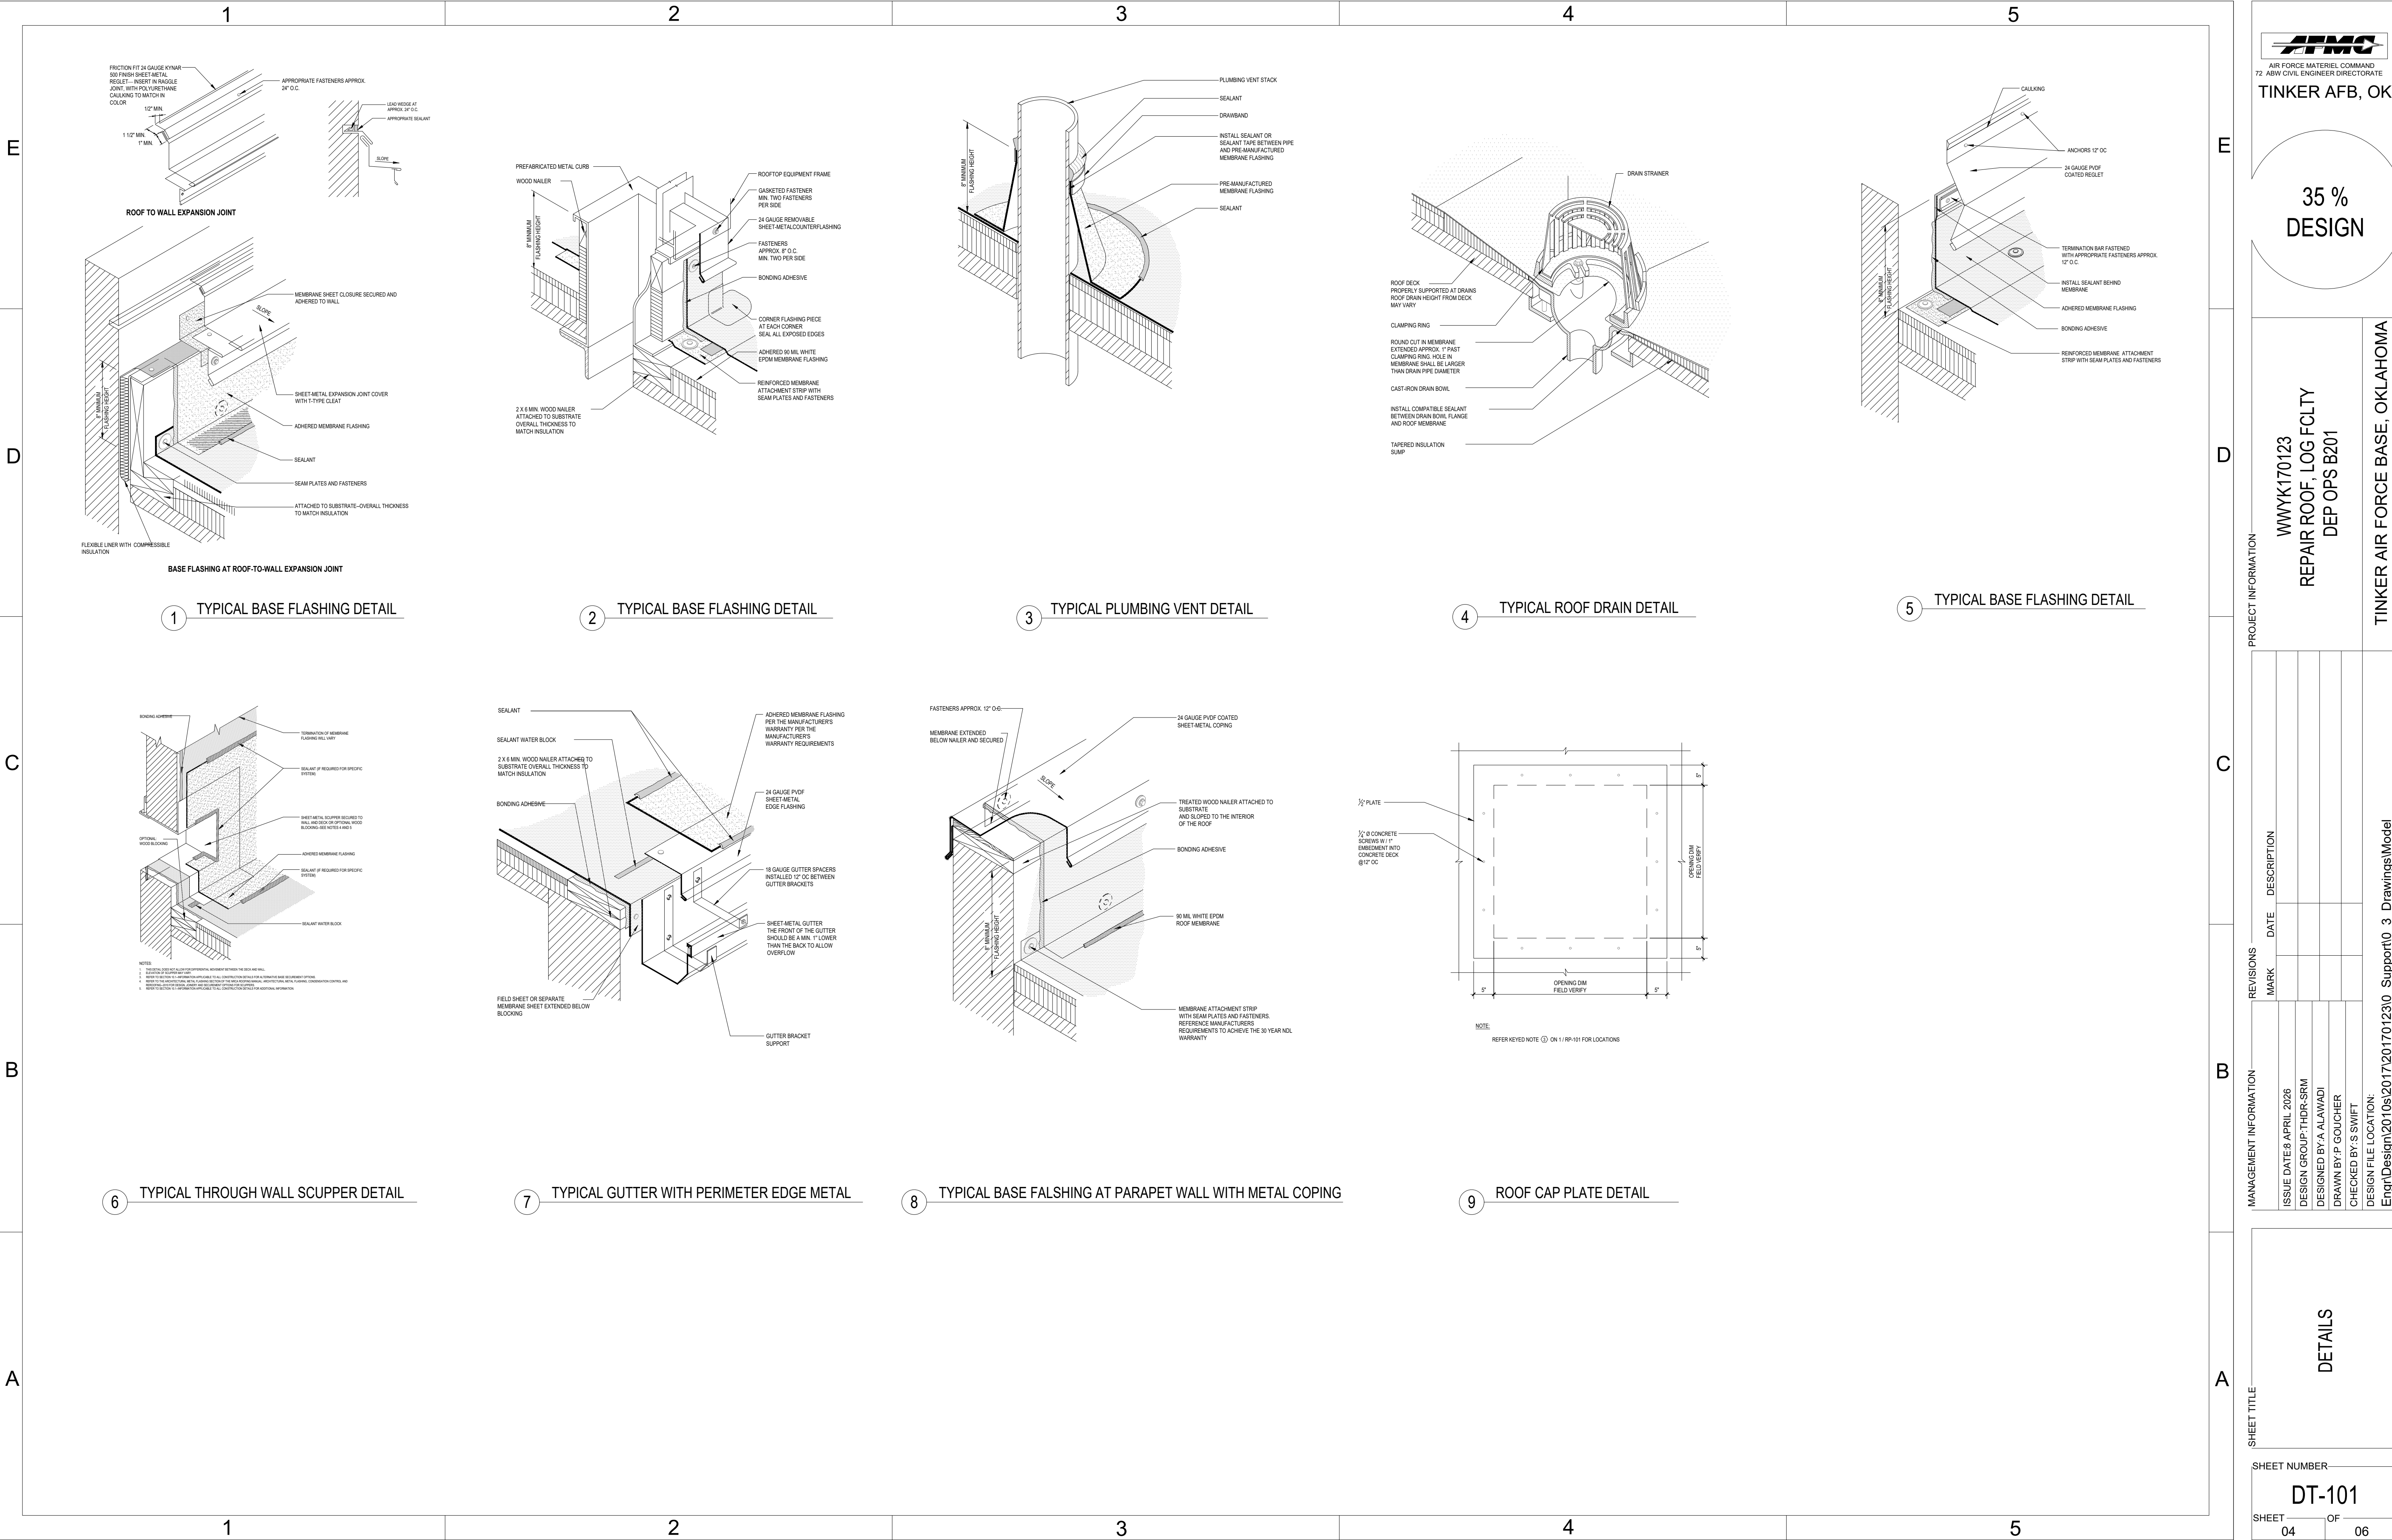

AIR FORCE MATERIEL COMMAND
72 ARMY CIVIL ENGINEER DIRECTORATE
TINKER AFB, OK


35 %
DESIGN

PROJECT INFORMATION
WWYK170123
REPAIR ROOF LOG FCULTY
DEP OPS B201
TINKER AIR FORCE BASE, OKLAHOMA

MANAGEMENT INFORMATION		REVISIONS		DATE		DESCRIPTION	
ISSUE DATE	8 APRIL 2026	MARK		DATE		DESCRIPTION	
DESIGN GROUP	THDR-GRM						
DESIGNED BY	A ALAWADI						
DRAWN BY	P GOUCHER						
CHECKED BY	S SWIFT						
DESIGN FILE LOCATION: Engr\Design\2010s\2017\20170123\0_Support0_3_DrawingsModel							


DETAILS

SHEET NUMBER
DT-101
SHEET 04 OF 06

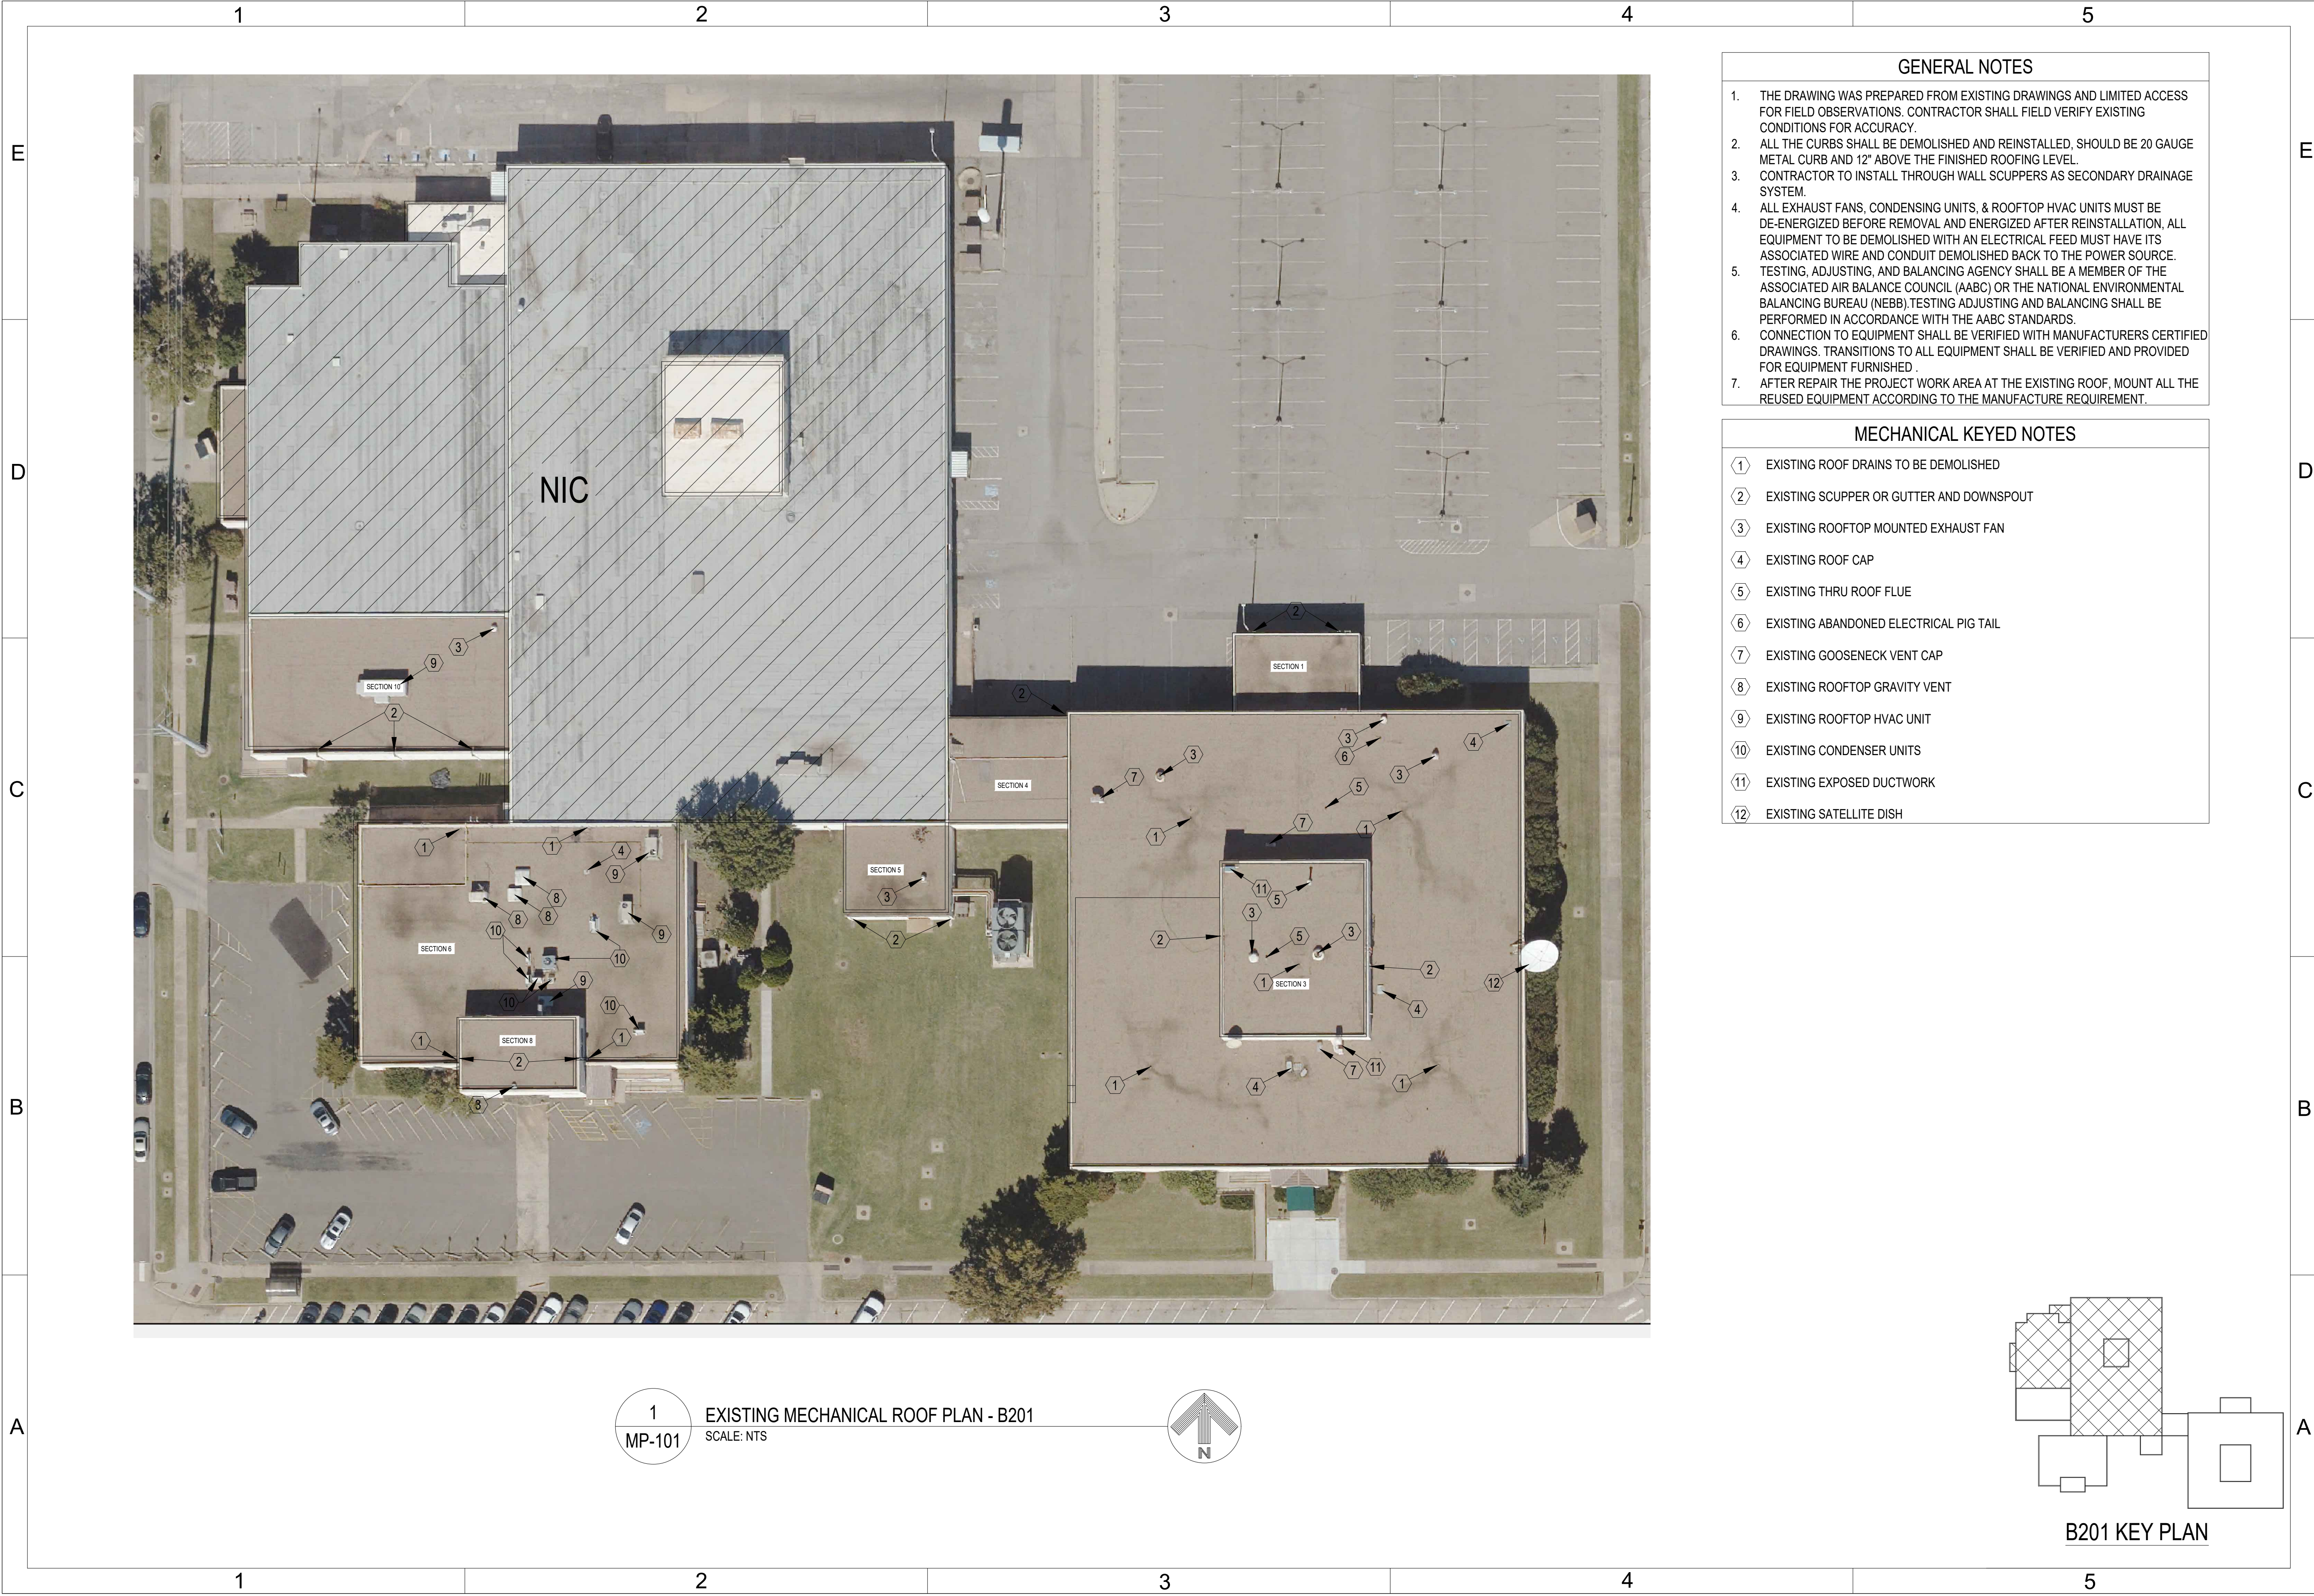

- GENERAL NOTES**
1. THE DRAWING WAS PREPARED FROM EXISTING DRAWINGS AND LIMITED ACCESS FOR FIELD OBSERVATIONS. CONTRACTOR SHALL FIELD VERIFY EXISTING CONDITIONS FOR ACCURACY.
 2. ALL THE CURBS SHALL BE DEMOLISHED AND REINSTALLED, SHOULD BE 20 GAUGE METAL CURB AND 12" ABOVE THE FINISHED ROOFING LEVEL.
 3. CONTRACTOR TO INSTALL THROUGH WALL SCUPPERS AS SECONDARY DRAINAGE SYSTEM.
 4. ALL EXHAUST FANS, CONDENSING UNITS, & ROOFTOP HVAC UNITS MUST BE DE-ENERGIZED BEFORE REMOVAL AND ENERGIZED AFTER REINSTALLATION, ALL EQUIPMENT TO BE DEMOLISHED WITH AN ELECTRICAL FEED MUST HAVE ITS ASSOCIATED WIRE AND CONDUIT DEMOLISHED BACK TO THE POWER SOURCE.
 5. TESTING, ADJUSTING, AND BALANCING AGENCY SHALL BE A MEMBER OF THE ASSOCIATED AIR BALANCE COUNCIL (AABC) OR THE NATIONAL ENVIRONMENTAL BALANCING BUREAU (NEBB). TESTING ADJUSTING AND BALANCING SHALL BE PERFORMED IN ACCORDANCE WITH THE AABC STANDARDS.
 6. CONNECTION TO EQUIPMENT SHALL BE VERIFIED WITH MANUFACTURERS CERTIFIED DRAWINGS. TRANSITIONS TO ALL EQUIPMENT SHALL BE VERIFIED AND PROVIDED FOR EQUIPMENT FURNISHED.
 7. AFTER REPAIR THE PROJECT WORK AREA AT THE EXISTING ROOF, MOUNT ALL THE REUSED EQUIPMENT ACCORDING TO THE MANUFACTURE REQUIREMENT.

- MECHANICAL KEYED NOTES**
- ① EXISTING ROOF DRAINS TO BE DEMOLISHED
 - ② EXISTING SCUPPER OR GUTTER AND DOWNSPOUT
 - ③ EXISTING ROOFTOP MOUNTED EXHAUST FAN
 - ④ EXISTING ROOF CAP
 - ⑤ EXISTING THRU ROOF FLUE
 - ⑥ EXISTING ABANDONED ELECTRICAL PIG TAIL
 - ⑦ EXISTING GOOSENECK VENT CAP
 - ⑧ EXISTING ROOFTOP GRAVITY VENT
 - ⑨ EXISTING ROOFTOP HVAC UNIT
 - ⑩ EXISTING CONDENSER UNITS
 - ⑪ EXISTING EXPOSED DUCTWORK
 - ⑫ EXISTING SATELLITE DISH

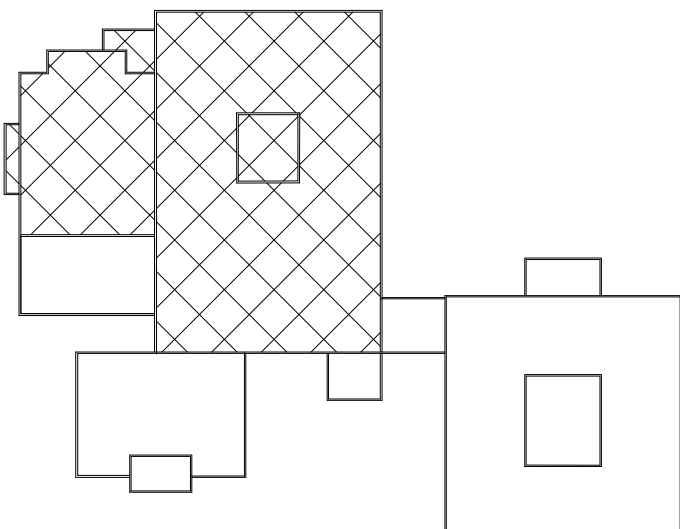

B201 KEY PLAN



AIR FORCE MATERIEL COMMAND
72 ABW CIVIL ENGINEER DIRECTORATE
TINKER AFB, OK

**35 %
DESIGN**

PROJECT INFORMATION

WWYK170123
REPAIR ROOF, LOG FCLTY
DEP OPS B201

TINKER AIR FORCE BASE, OKLAHOMA

MANAGEMENT INFORMATION		REVISIONS	
ISSUE	DATE	MARK	DESCRIPTION
DESIGN GROUP	TEPA-SRM		
DESIGNED BY	Q GAUNA		
DRAWN BY	P GOUCHER		
CHECKED BY	S SWIFT		
DESIGN FILE LOCATION: Engr\Design\20105\2017\20170123\0_Support\0_3_Drawings\Model			


SHEET TITLE

**EXISTING
MECHANICAL
ROOF PLAN - B201**


SHEET NUMBER

MP-101

SHEET 05 OF 06

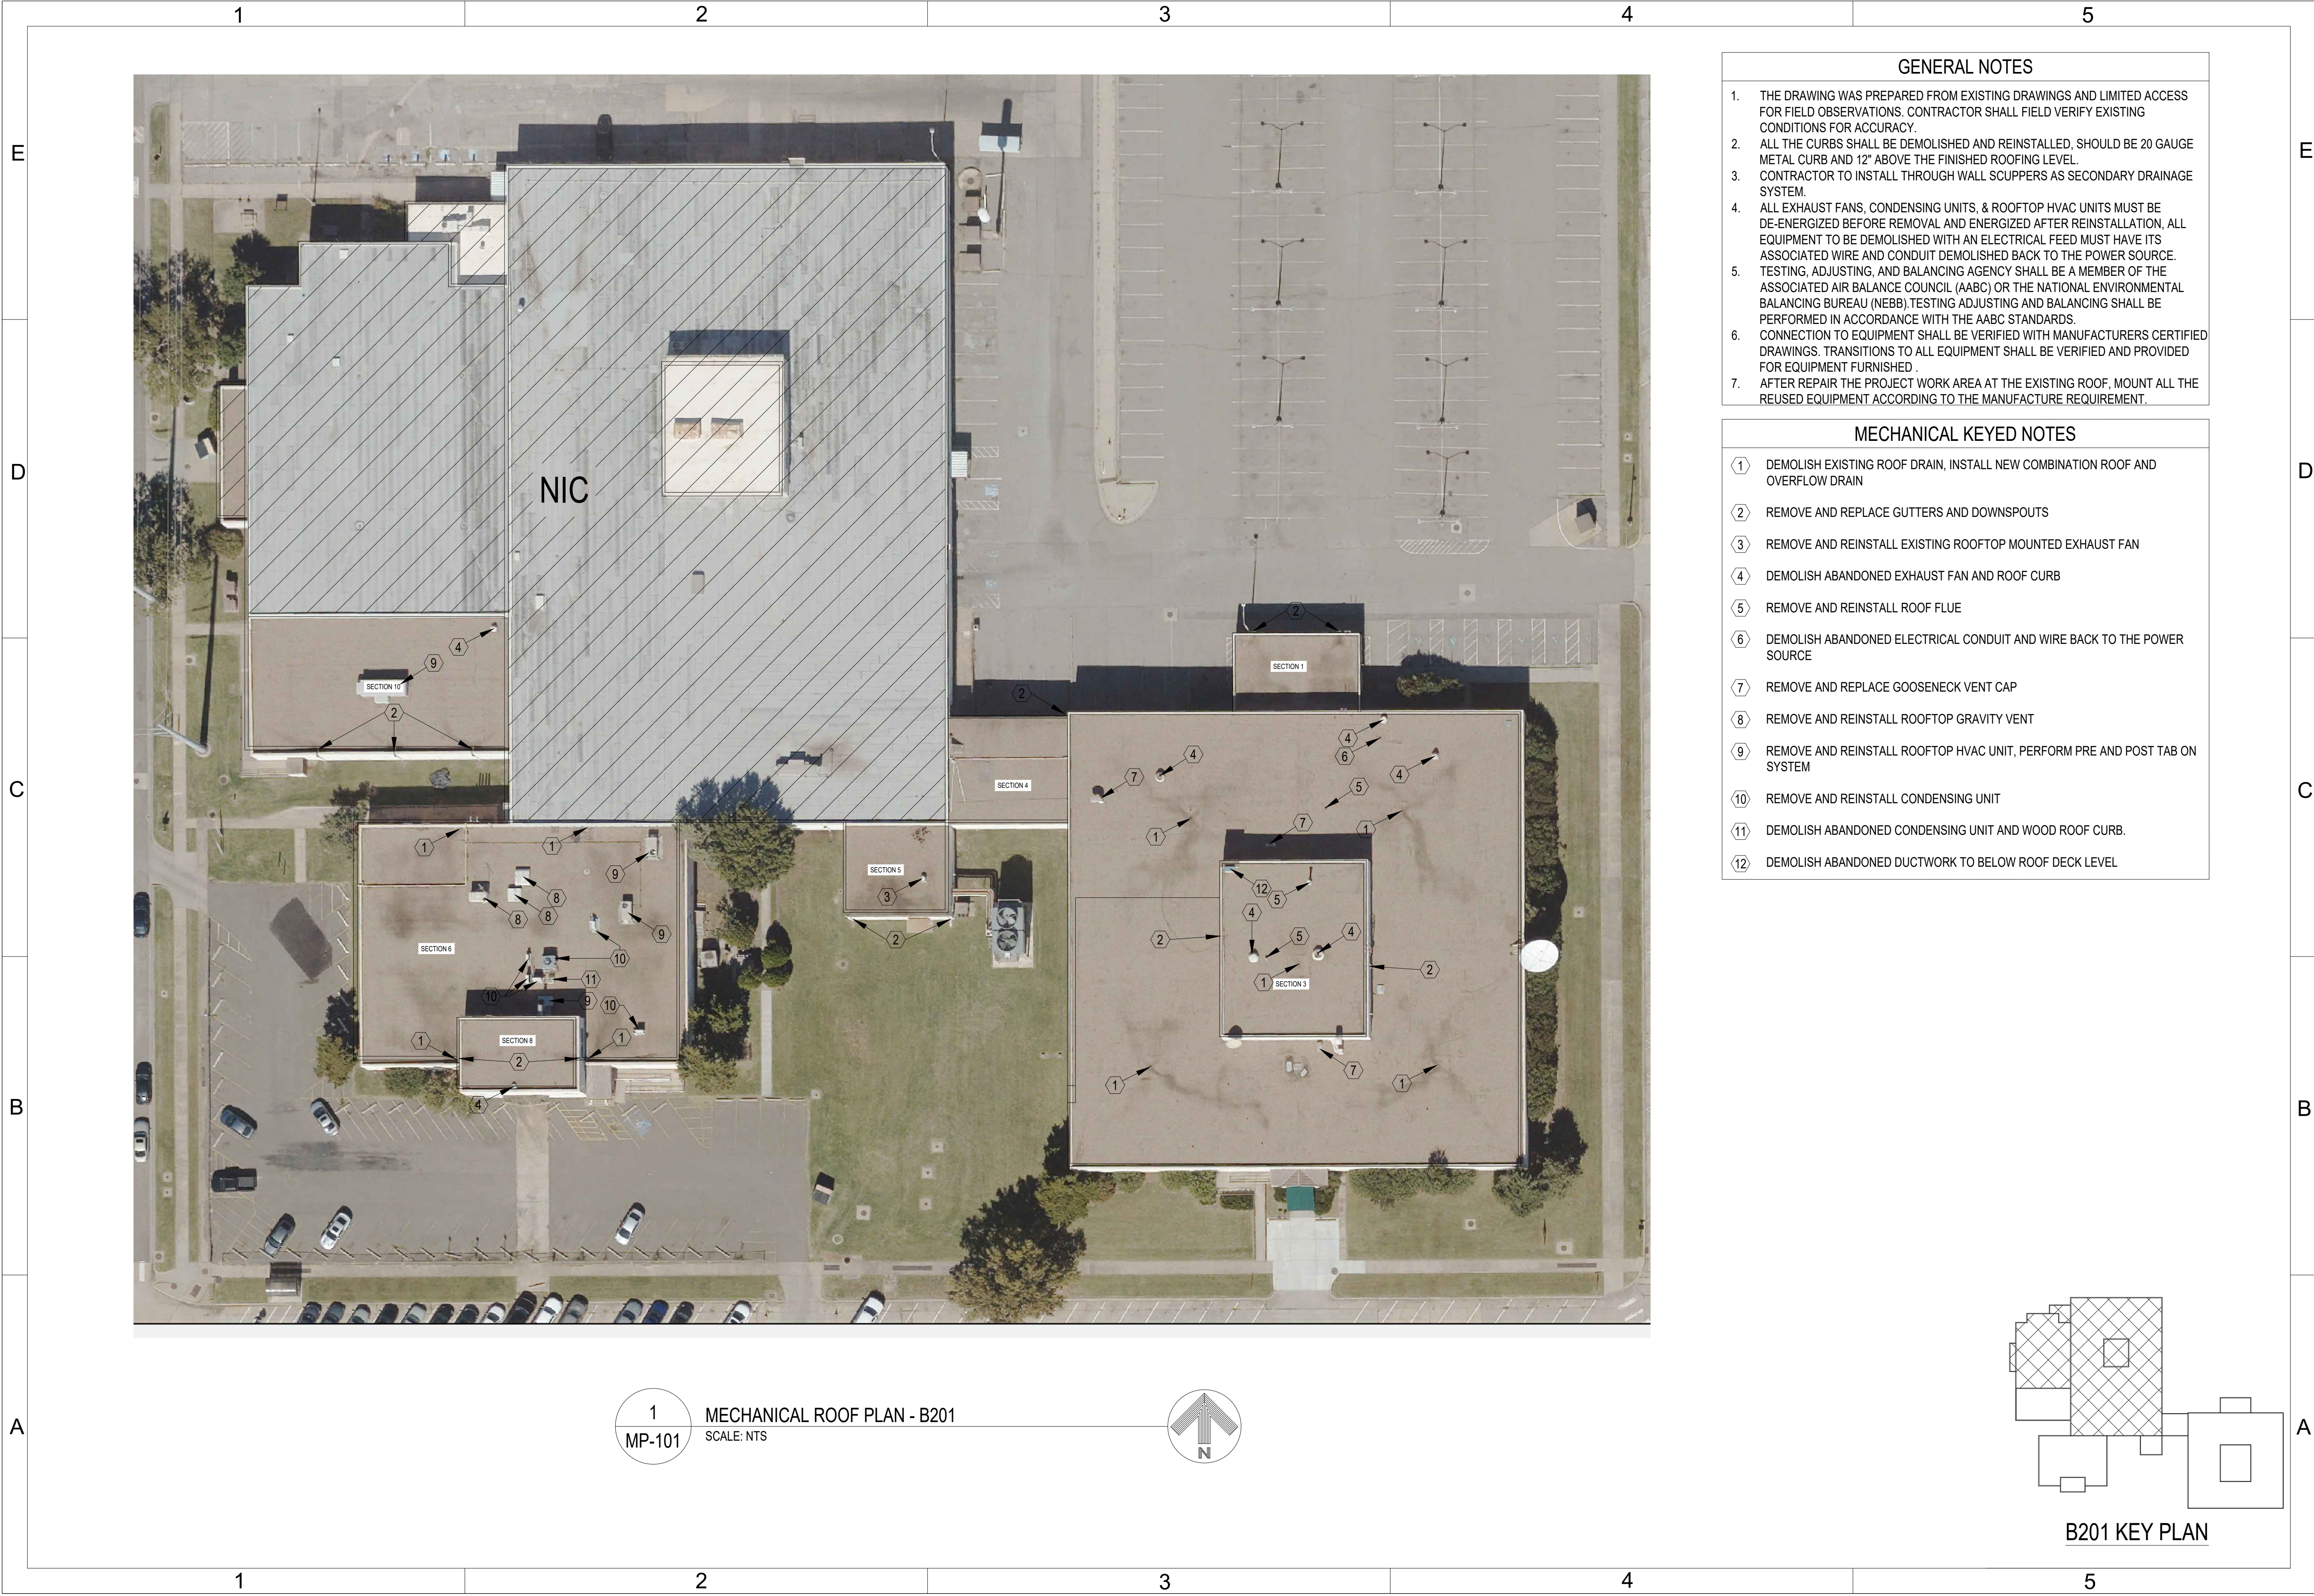


1
MP-101
MECHANICAL ROOF PLAN - B201
SCALE: NTS

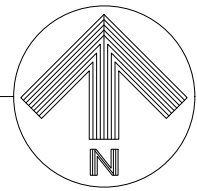

- ### GENERAL NOTES
1. THE DRAWING WAS PREPARED FROM EXISTING DRAWINGS AND LIMITED ACCESS FOR FIELD OBSERVATIONS. CONTRACTOR SHALL FIELD VERIFY EXISTING CONDITIONS FOR ACCURACY.
 2. ALL THE CURBS SHALL BE DEMOLISHED AND REINSTALLED, SHOULD BE 20 GAUGE METAL CURB AND 12" ABOVE THE FINISHED ROOFING LEVEL.
 3. CONTRACTOR TO INSTALL THROUGH WALL SCUPPERS AS SECONDARY DRAINAGE SYSTEM.
 4. ALL EXHAUST FANS, CONDENSING UNITS, & ROOFTOP HVAC UNITS MUST BE DE-ENERGIZED BEFORE REMOVAL AND ENERGIZED AFTER REINSTALLATION, ALL EQUIPMENT TO BE DEMOLISHED WITH AN ELECTRICAL FEED MUST HAVE ITS ASSOCIATED WIRE AND CONDUIT DEMOLISHED BACK TO THE POWER SOURCE.
 5. TESTING, ADJUSTING, AND BALANCING AGENCY SHALL BE A MEMBER OF THE ASSOCIATED AIR BALANCE COUNCIL (AABC) OR THE NATIONAL ENVIRONMENTAL BALANCING BUREAU (NEBB). TESTING ADJUSTING AND BALANCING SHALL BE PERFORMED IN ACCORDANCE WITH THE AABC STANDARDS.
 6. CONNECTION TO EQUIPMENT SHALL BE VERIFIED WITH MANUFACTURERS CERTIFIED DRAWINGS. TRANSITIONS TO ALL EQUIPMENT SHALL BE VERIFIED AND PROVIDED FOR EQUIPMENT FURNISHED.
 7. AFTER REPAIR THE PROJECT WORK AREA AT THE EXISTING ROOF, MOUNT ALL THE REUSED EQUIPMENT ACCORDING TO THE MANUFACTURE REQUIREMENT.

- ### MECHANICAL KEYED NOTES
- ① DEMOLISH EXISTING ROOF DRAIN, INSTALL NEW COMBINATION ROOF AND OVERFLOW DRAIN
 - ② REMOVE AND REPLACE GUTTERS AND DOWNSPOUTS
 - ③ REMOVE AND REINSTALL EXISTING ROOFTOP MOUNTED EXHAUST FAN
 - ④ DEMOLISH ABANDONED EXHAUST FAN AND ROOF CURB
 - ⑤ REMOVE AND REINSTALL ROOF FLUE
 - ⑥ DEMOLISH ABANDONED ELECTRICAL CONDUIT AND WIRE BACK TO THE POWER SOURCE
 - ⑦ REMOVE AND REPLACE GOOSENECK VENT CAP
 - ⑧ REMOVE AND REINSTALL ROOFTOP GRAVITY VENT
 - ⑨ REMOVE AND REINSTALL ROOFTOP HVAC UNIT, PERFORM PRE AND POST TAB ON SYSTEM
 - ⑩ REMOVE AND REINSTALL CONDENSING UNIT
 - ⑪ DEMOLISH ABANDONED CONDENSING UNIT AND WOOD ROOF CURB.
 - ⑫ DEMOLISH ABANDONED DUCTWORK TO BELOW ROOF DECK LEVEL

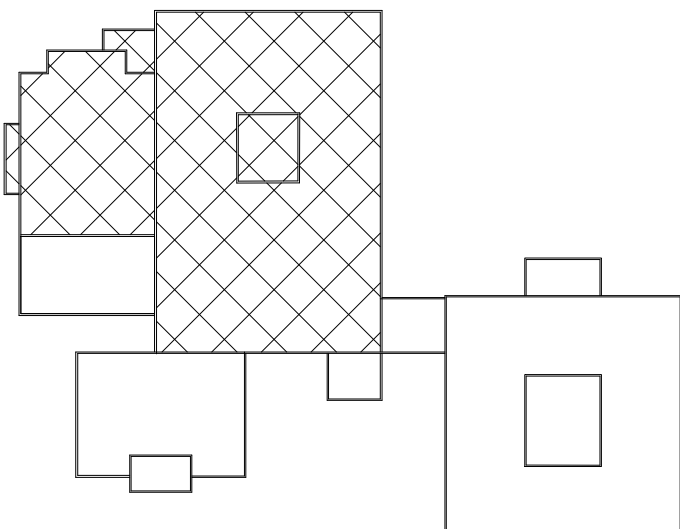

B201 KEY PLAN

AIR FORCE MATERIEL COMMAND
72 ABW CIVIL ENGINEER DIRECTORATE
TINKER AFB, OK

35 %
DESIGN

PROJECT INFORMATION

WWYK170123
REPAIR ROOF, LOG FCULTY
DEP OPS B201

TINKER AIR FORCE BASE, OKLAHOMA

MANAGEMENT INFORMATION		REVISIONS	
ISSUE	DATE	MARK	DESCRIPTION
DESIGN GROUP	TEPA-SRM		
DESIGNED BY	Q. GAUNA		
DRAWN BY	P. GOUCHER		
CHECKED BY	S. SWIFT		
DESIGN FILE LOCATION: Engr\Design\20105\2017\20170123\0_Support\0_3_Drawings\Model			

SHEET TITLE

MECHANICAL
ROOF PLAN - B201

SHEET NUMBER

MP-102

SHEET	06	OF	06
-------	----	----	----