


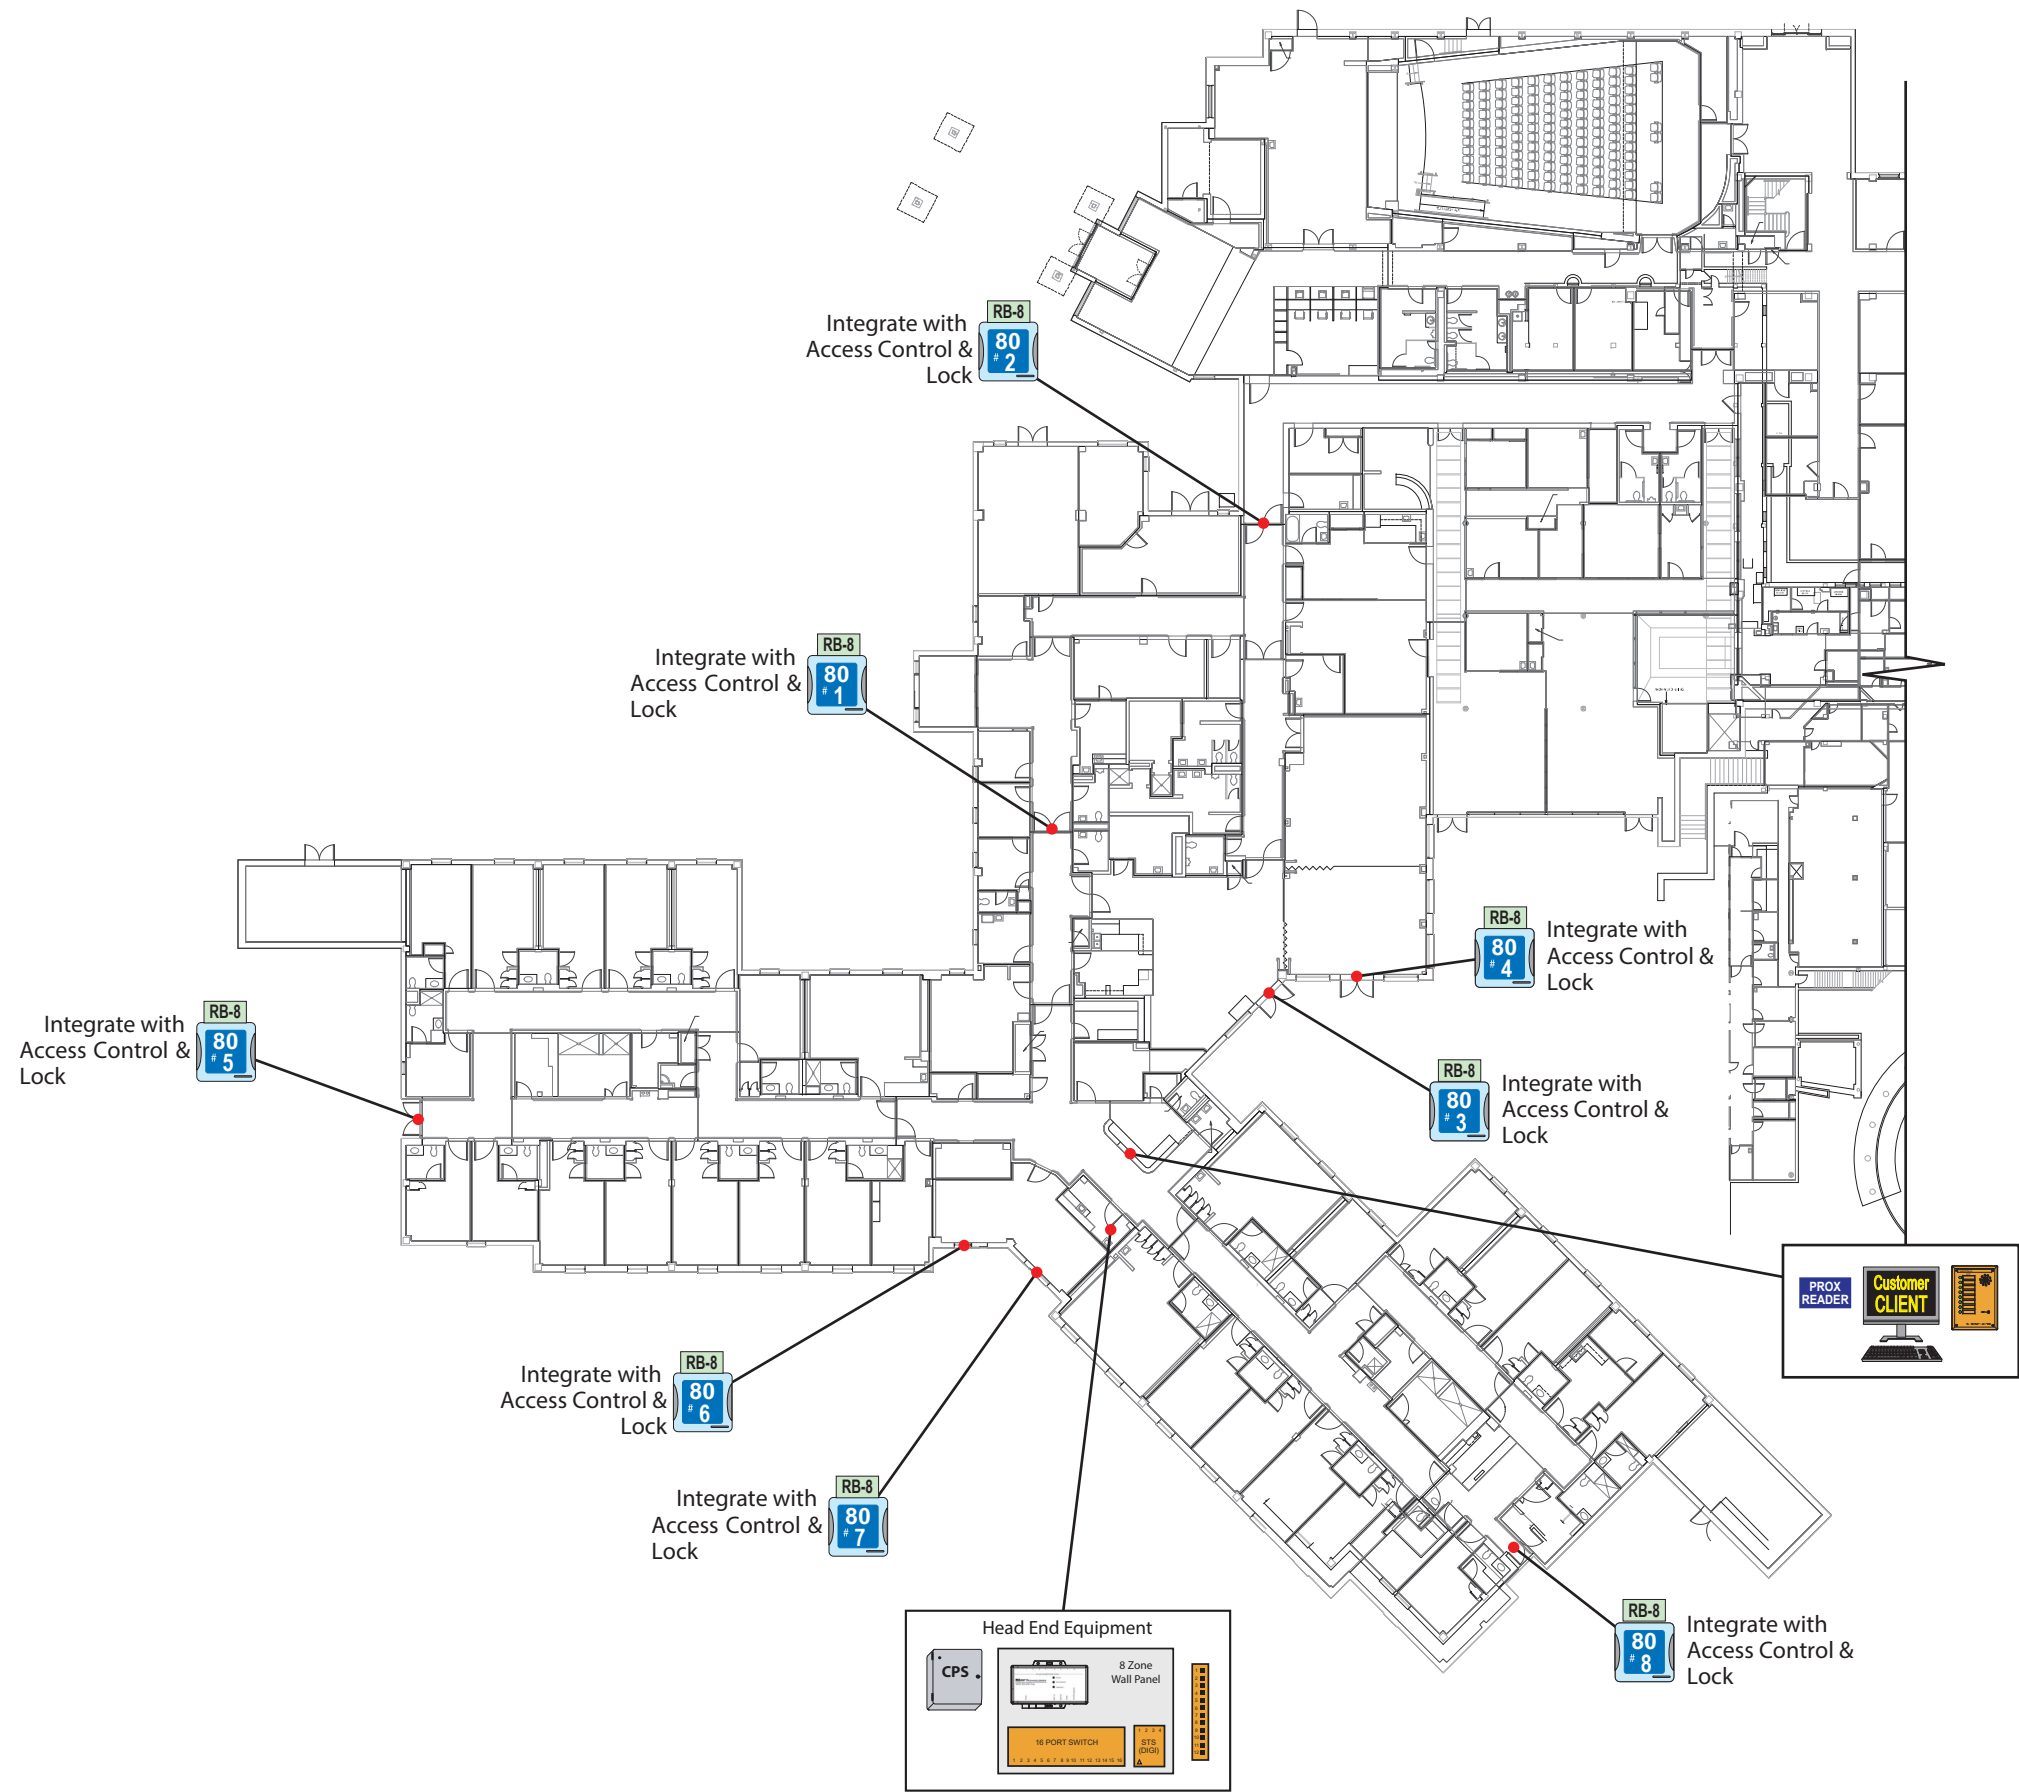

9450 SYSTEM - DEVICE LEGEND



Single Model
Touchpad Exit Controller (TEC)

Qty. 8



Deactivation Relay

Qty. 8



Virtualized Server



Client PC



Staff Alert Panel 8-Zone



Proximity Card Reader (PC)



Central Power Supply



Hub



Serial Terminal Server



Switch Box Patch Panel



Included in the 8 Zone Wall Panel

NOTE: All floor plans are configured with approximate device locations and are subject to change.

Rev	Date	Initials


Wilmington VA Medical Center
Wilmington, DE
CLC Patient Area
Device Layout

System: 9450 Wander Management w/ ID	Date: 11/07/25	Sheet: 1 of 2
Drawn By: M. Dawson	Rev: 0	

Copyright © RF Technologies 2025



Virtualized Server
(on Hospital Hardware/Network)

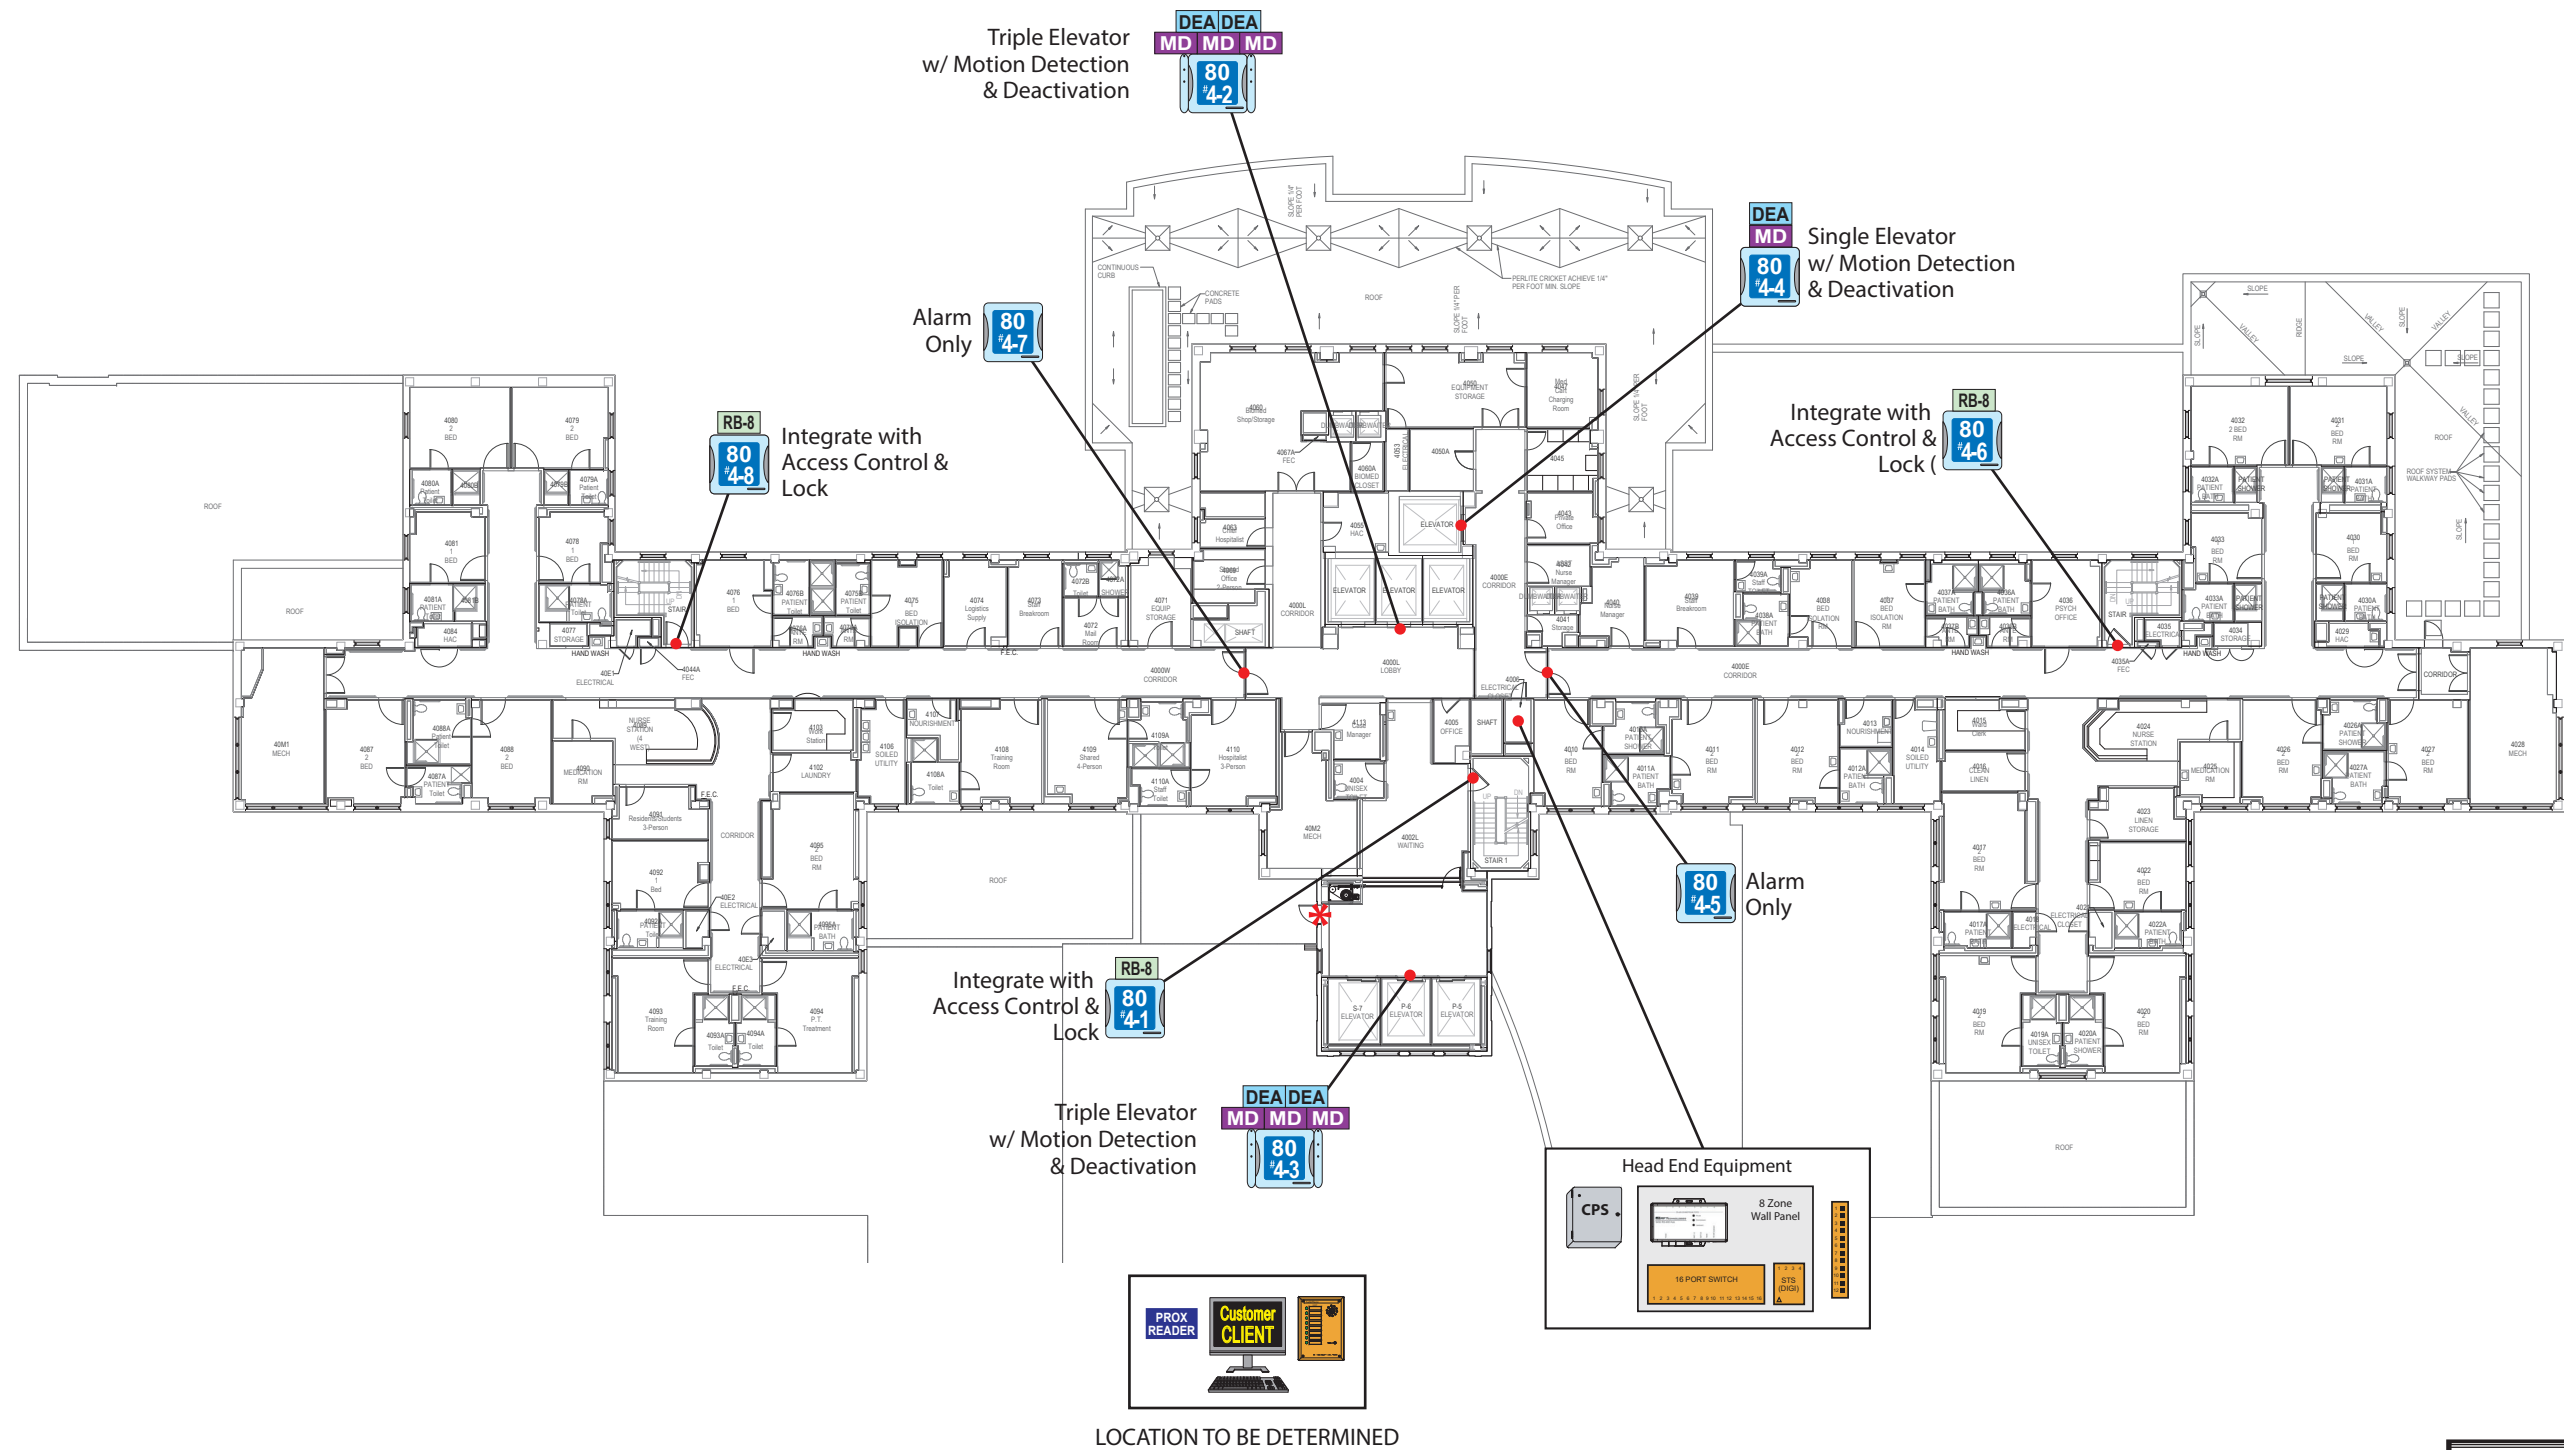

9450 SYSTEM - DEVICE LEGEND



Single Model
Touchpad Exit Controller (TEC)

Qty. 8



Exit Alarm Reciever Kit

Qty. 4



Deactivation Relay Motion

Qty. 3



Detector, Door/Hallway

Qty. 7



Elevator Deactivation Relay

Qty. 5



Client PC



Staff Alert Panel 8-Zone



Proximity Card Reader (PC)



Central Power Supply



Hub



Serial Terminal Server



Switch Box



Patch Panel

Included in the 8 Zone Wall Panel

* Door locked or managed by facility

NOTE: All floor plans are configured with approximate device locations and are subject to change.			Wilmington VA Medical Center Wilmington, DE 4th Floor Area Device Layout		
Rev	Date	Initials			
System: 9450 Wander Management w/ ID			Date	11/07/25	Sheet 2 of 2
Copyright © RF Technologies 2025			Drawn By	M. Dawson	Rev 0