

Enlarged drawing set

Same non-proprietary concept drawings, reorganized onto more sheets for easier viewing.

Phoenix Indian Medical Center

Microbiology Lab

Readability edition

This version enlarges the room plans and detail views so the drawings are easier to read on screen and in print.

The content remains an independent concept package and does not reproduce source logos, ownership legends, or vendor title blocks.

Use these sheets for internal planning and coordination; final field verification and fabrication detailing are still required.

Viewing tip

For the clearest view, open the PDF at 125% to 200% zoom.

Each room plan and each elevation now has its own larger sheet.


Sheets in this enlarged set

- 01. Room 1 overall plan
- 02. Room 2 overall plan
- 03. Room 3 overall plan
- 04. Room 4 overall plan
- 05. Detail 1 - Room 1 L workstation elevation
- 06. Detail 2 - Room 1 worktable elevation
- 07. Detail 3 - Room 1 worktable elevation
- 08. Detail 4 - Room 2 fixed sink / flammable base
- 09. Detail 5 - Room 2 mobile workstation + support table
- 10. Detail 6 - Room 2 analyzer station
- 11. Detail 7 - Room 3 microscope bench elevation
- 12. Detail 8 - Room 3 analyzer stand
- 13. Detail 9 - Room 4 workstation elevation
- 14. Detail 10 - Room 4 analyzer table elevation

Room 1 overall plan

Wall shelving above worktables


Z-001

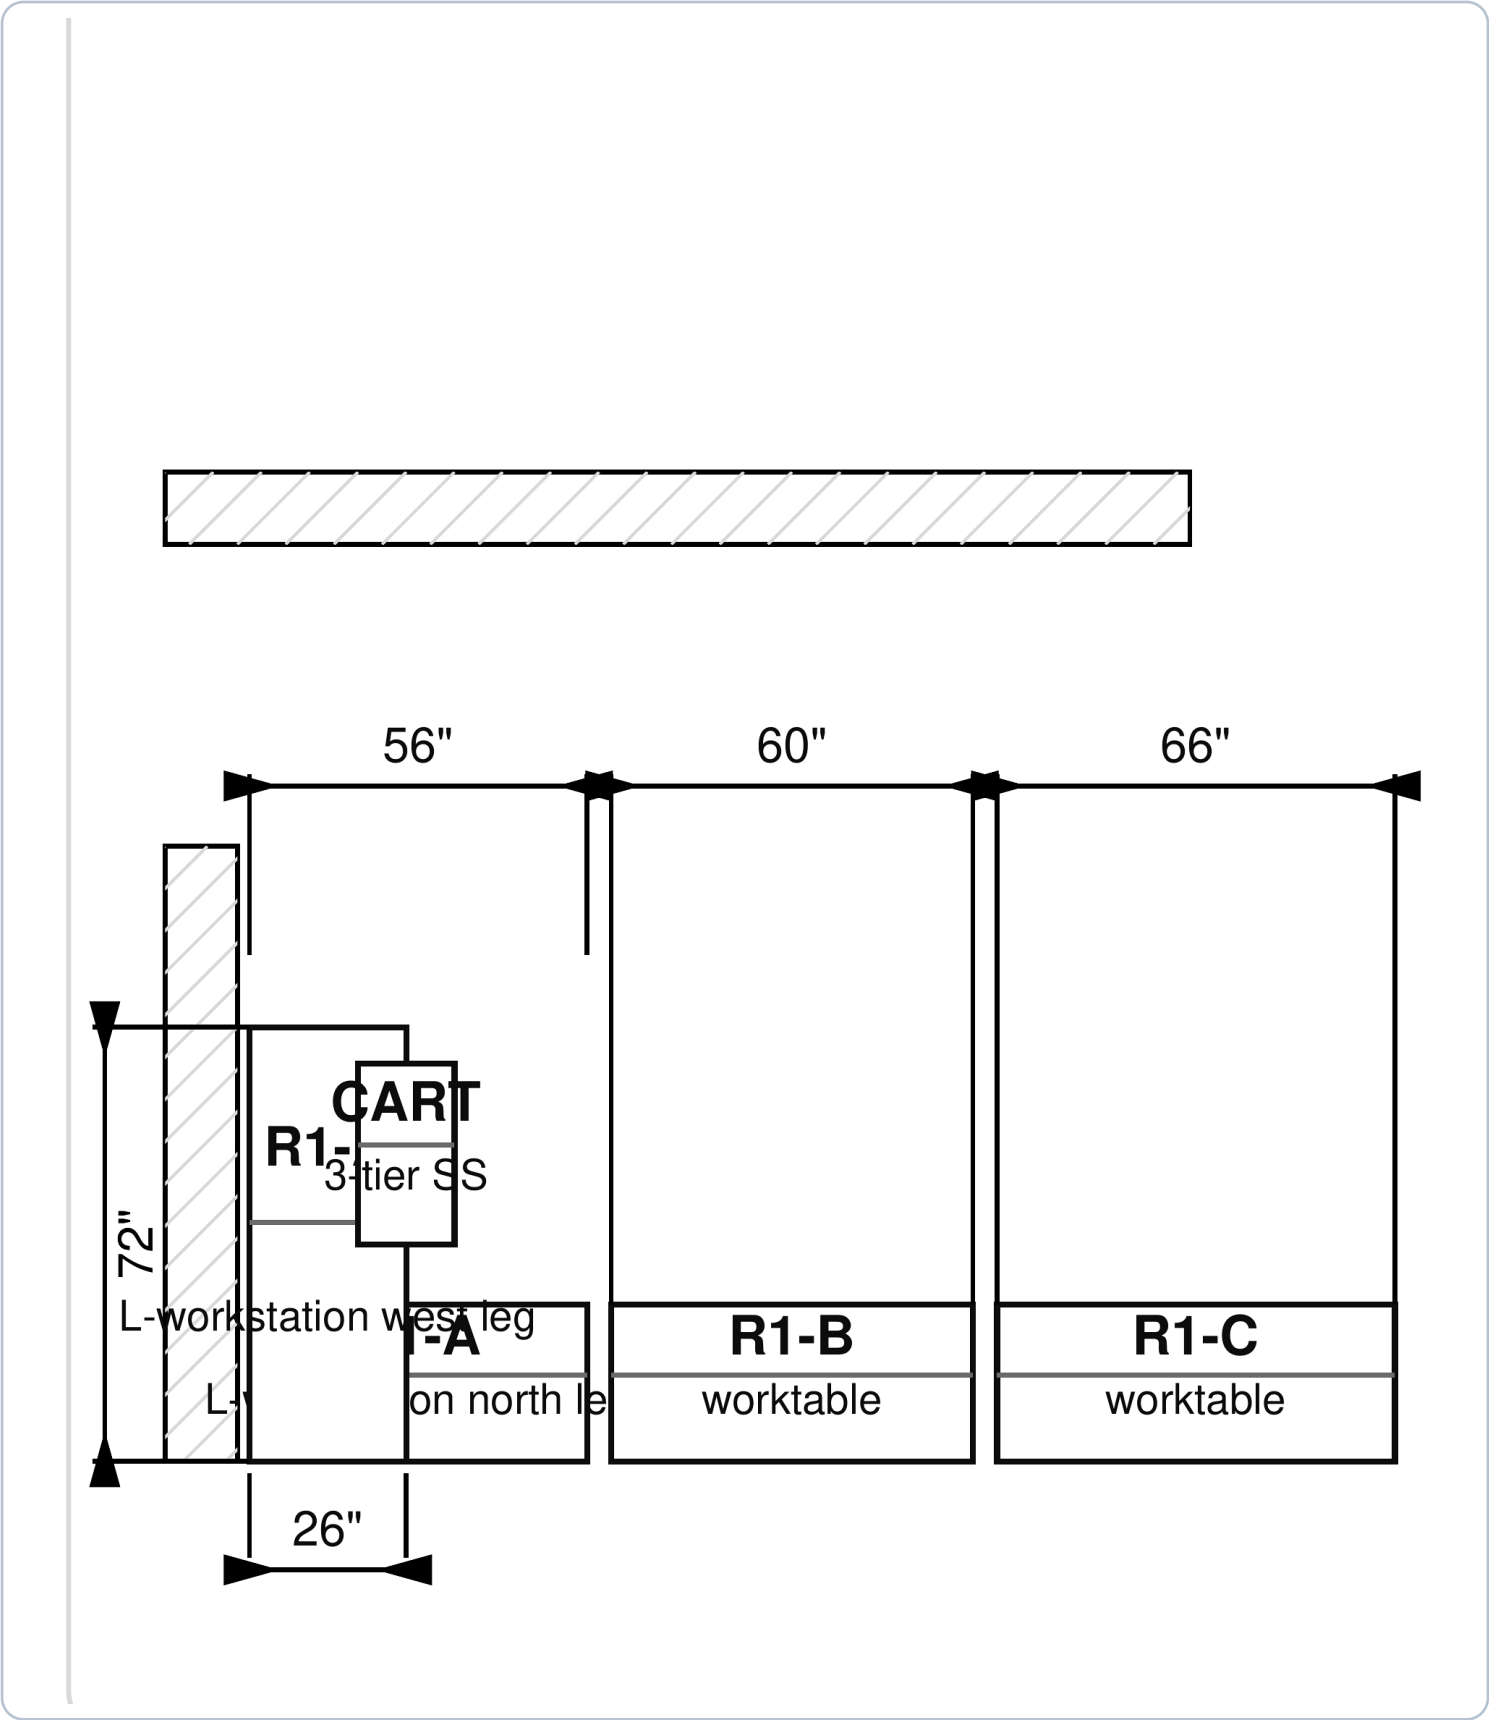

Room 2 overall plan

Z-002


Fixed sink base, mobile station, support table, analyzer station

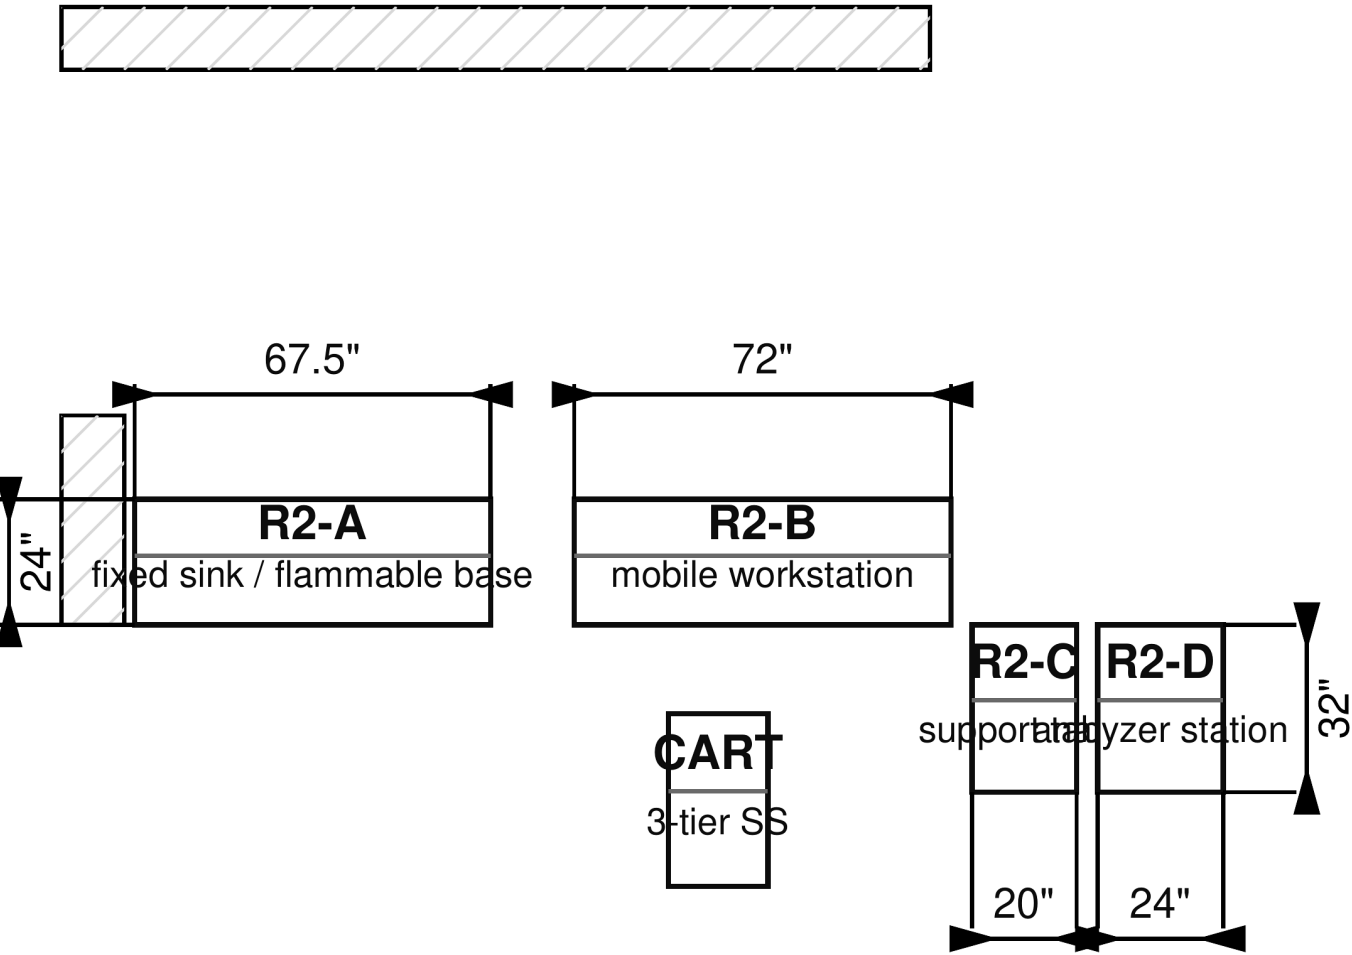

Room 3 overall plan

Two microscope benches and analyzer stand


Z-003

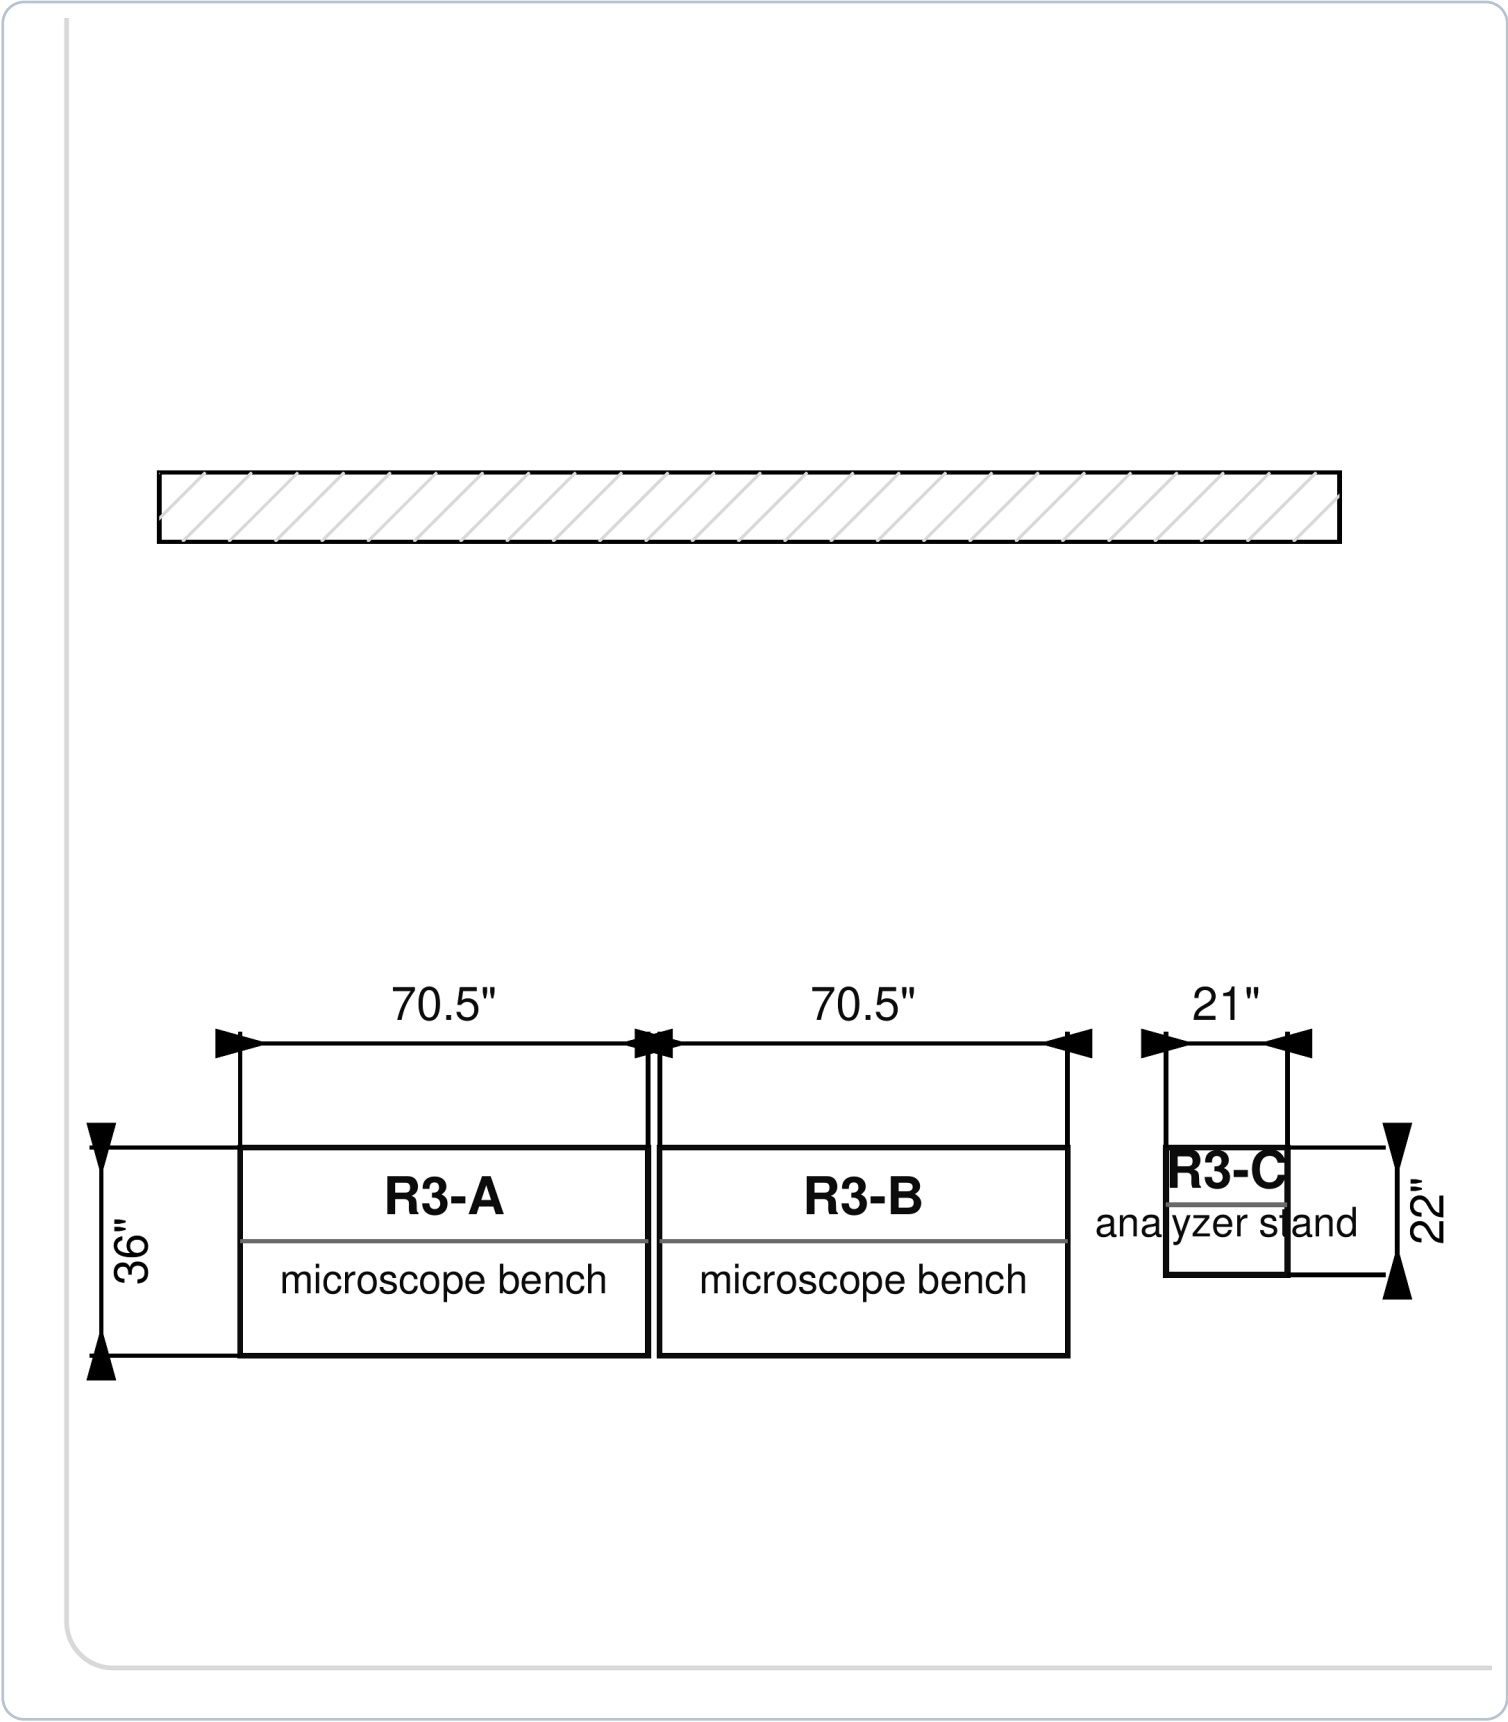

Room 4 overall plan

Main workstation and analyzer table


Z-004

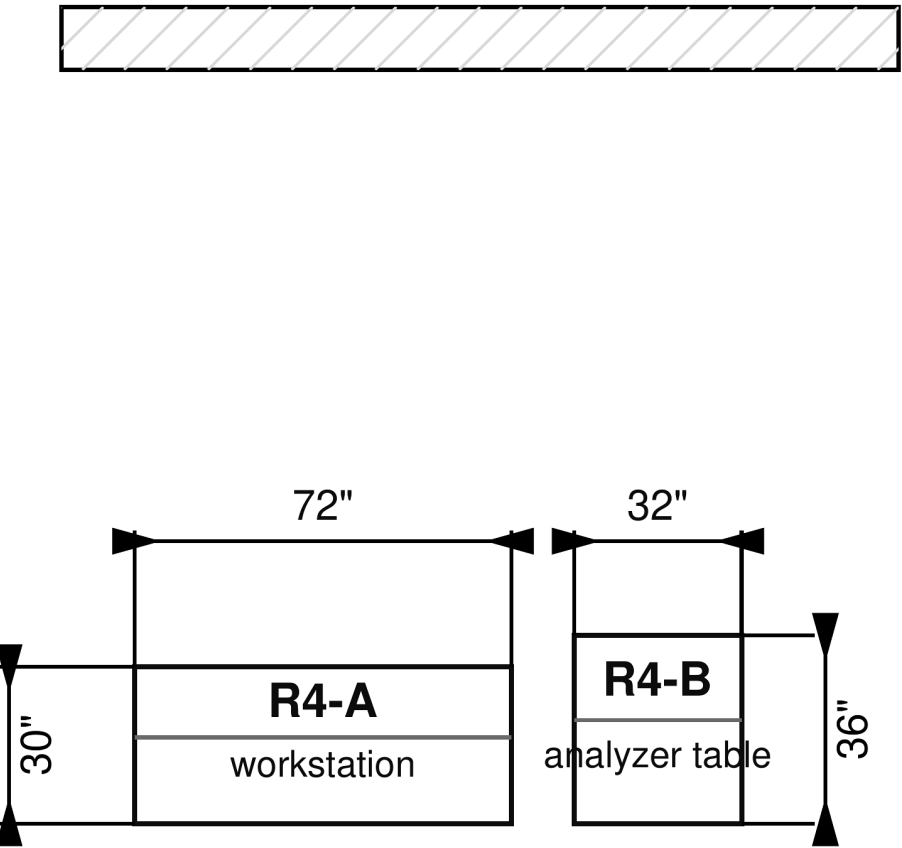

Detail 1 - Room 1 L workstation elevation

Z-005


Approx. 56 in nominal run; 41 in work height

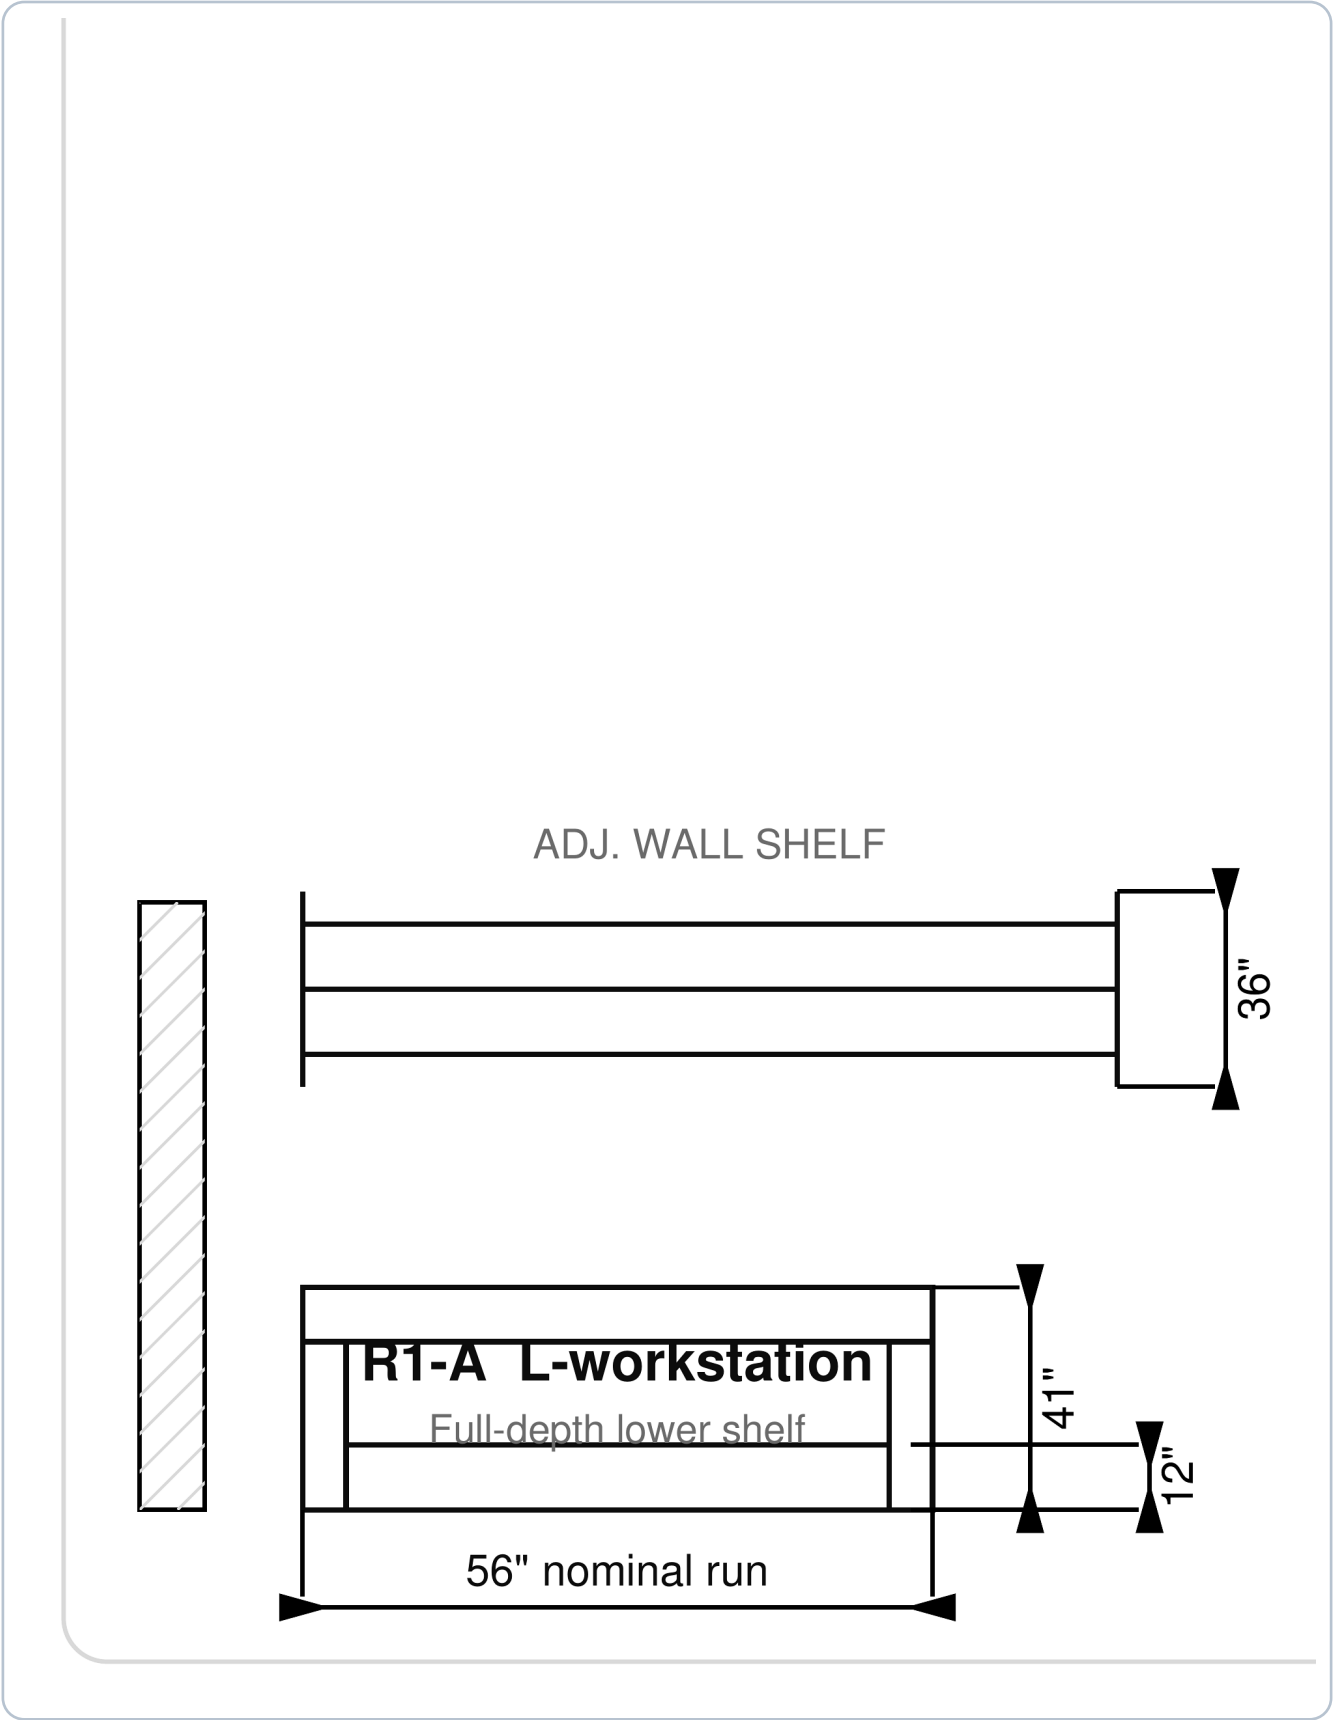

Detail 2 - Room 1 worktable elevation

Z-006


Approx. 60 x 26; adjustable wall shelf above

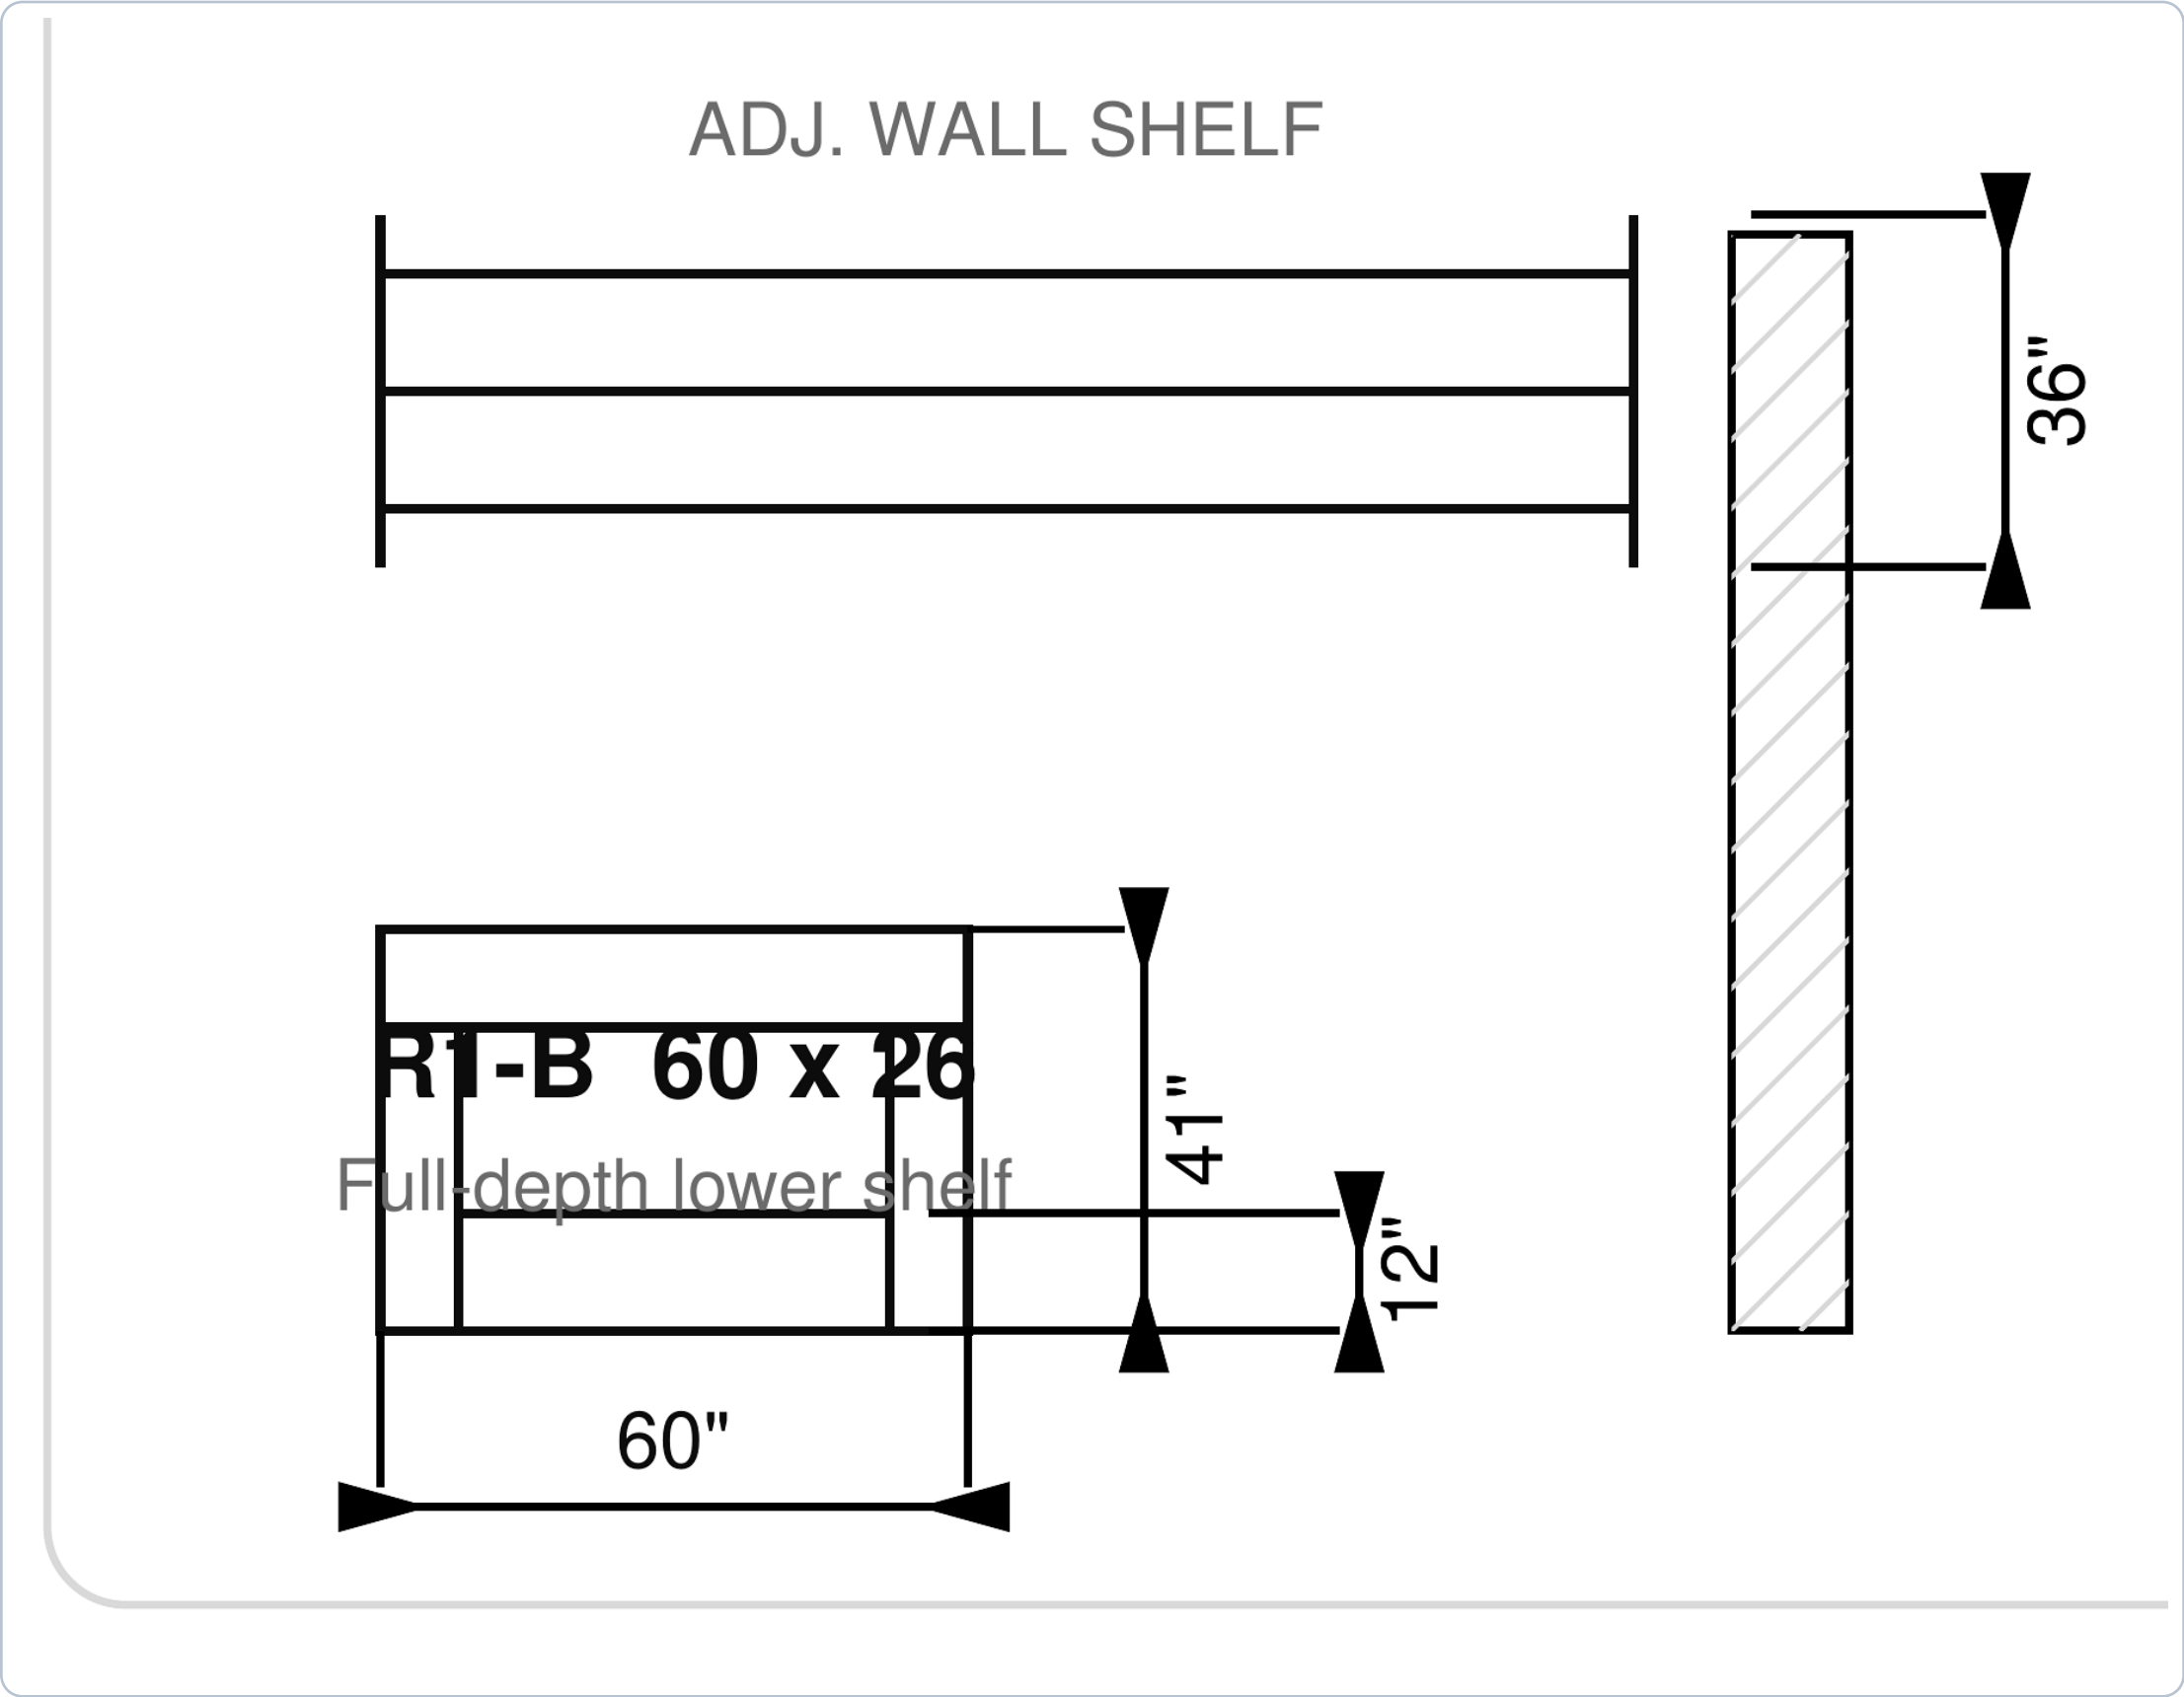

Detail 3 - Room 1 worktable elevation

Z-007


Approx. 66 x 26; adjustable wall shelf above

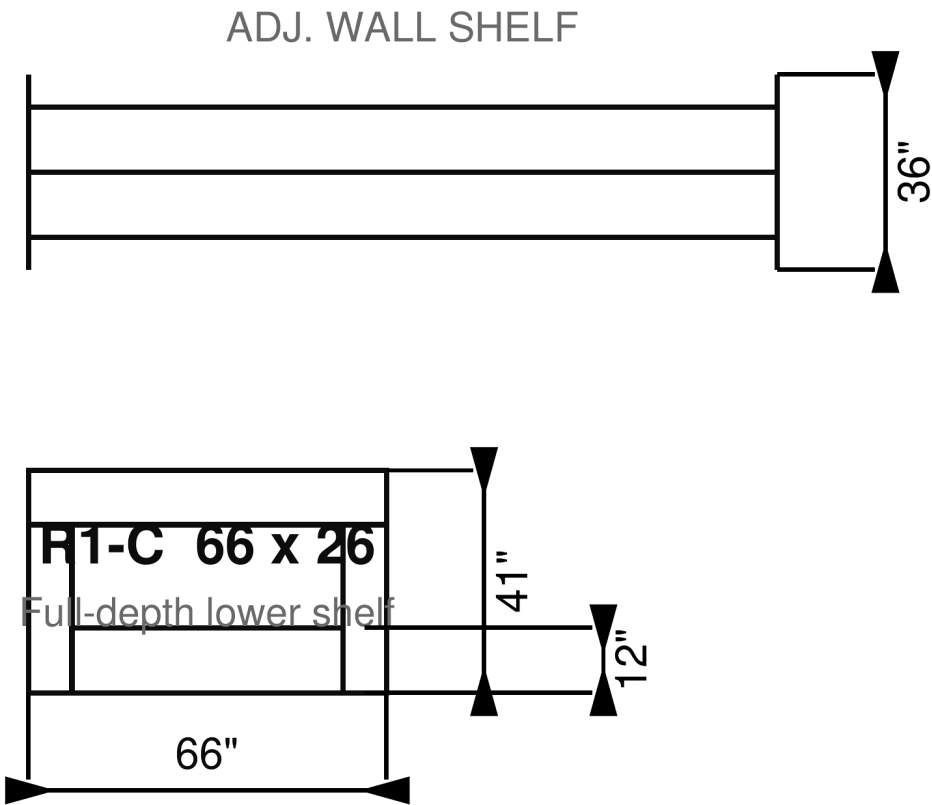

Detail 4 - Room 2 fixed sink / flammable base

Z-008


Approx. 67.5 x 24 fixed casework with integral sink top

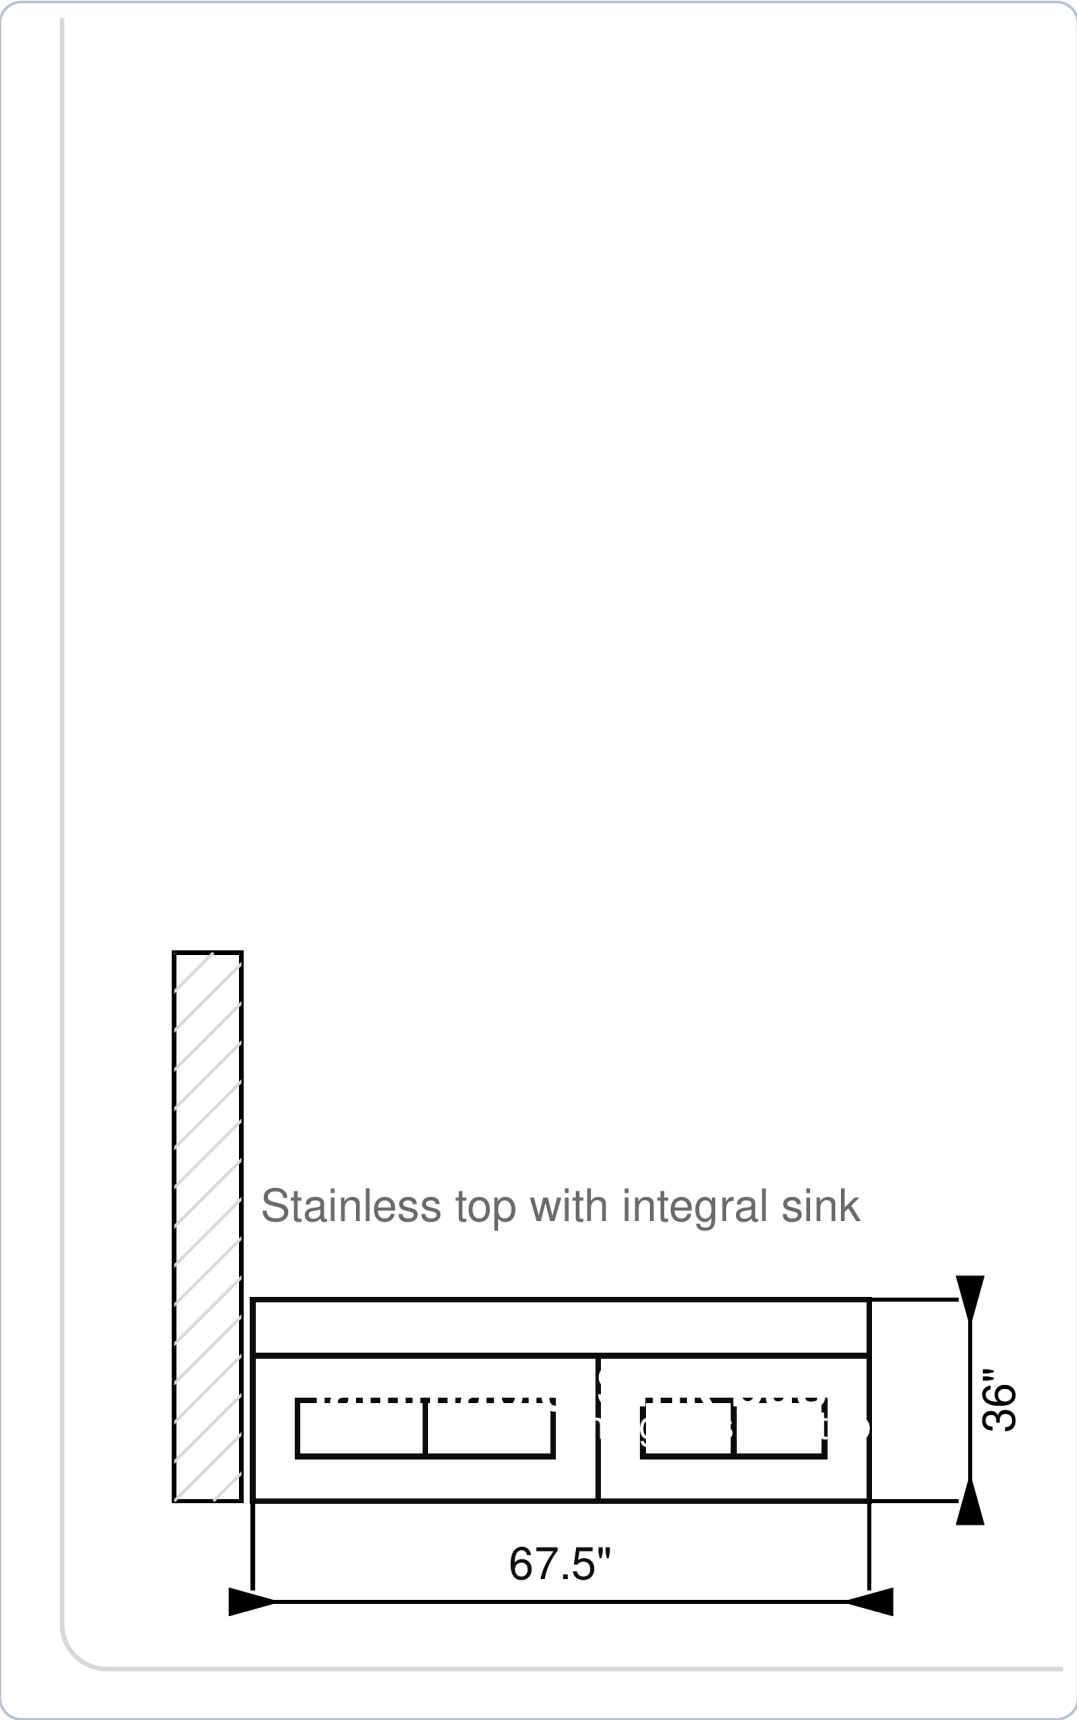

Detail 5 - Room 2 mobile workstation + support table

Z-009


Approx. 72 x 24 plus 20 x 24 support table

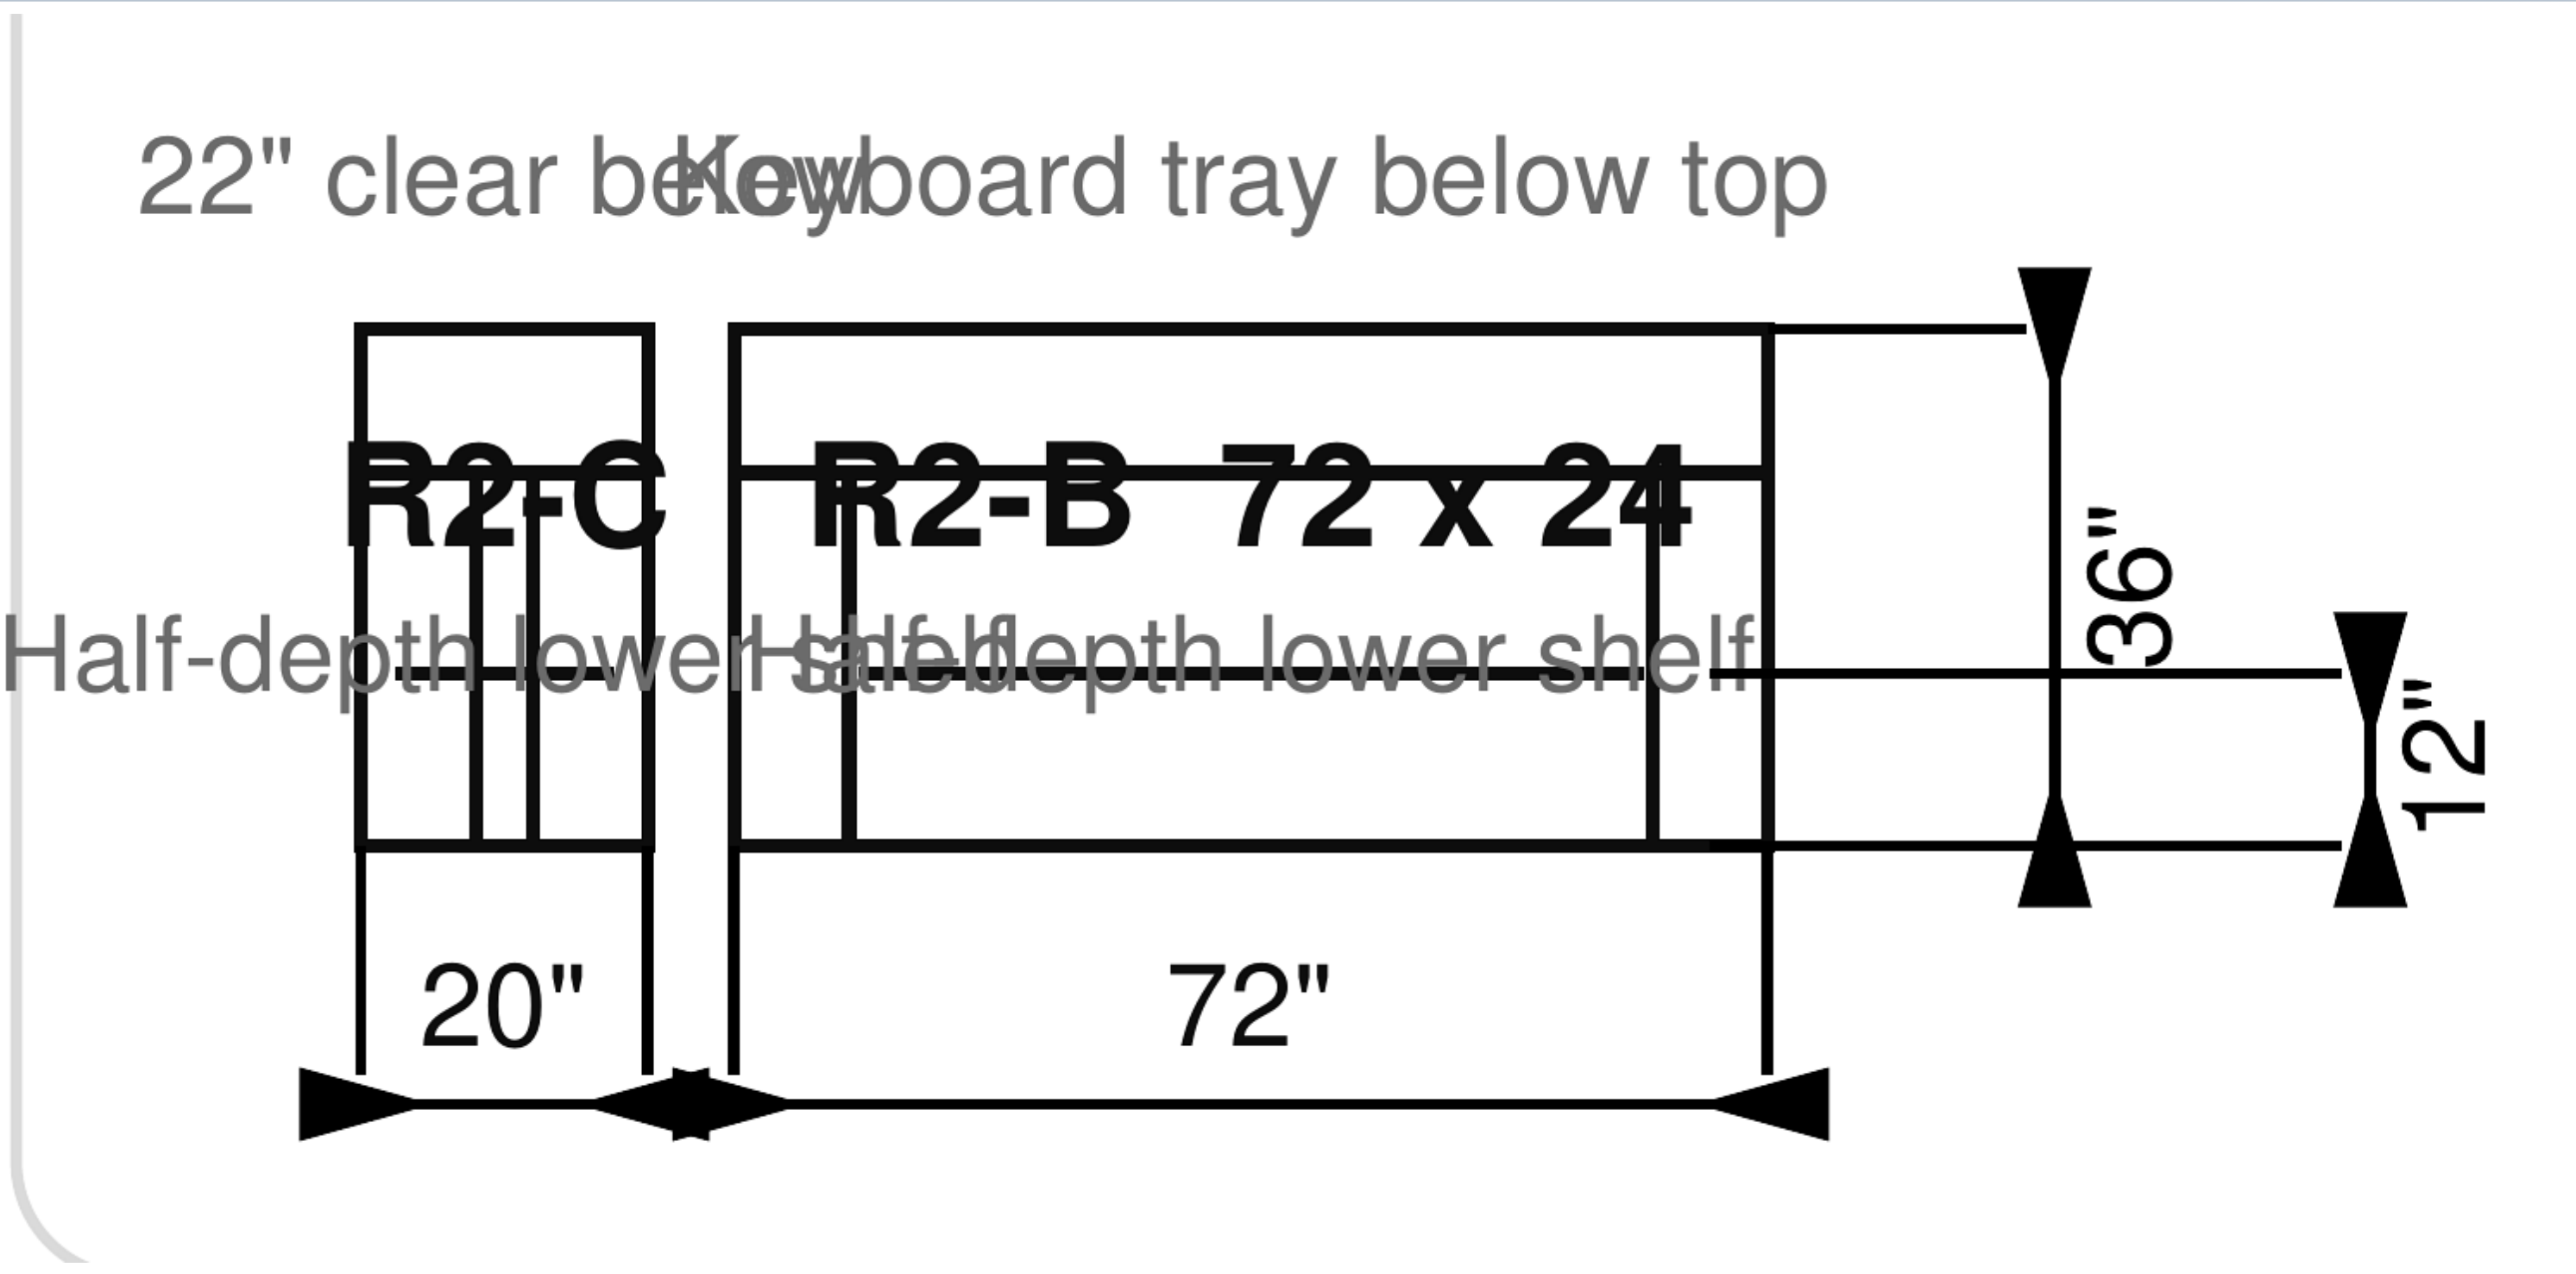

Detail 6 - Room 2 analyzer station

Z-010


Approx. 24 x 24 x 49 with two lower shelves

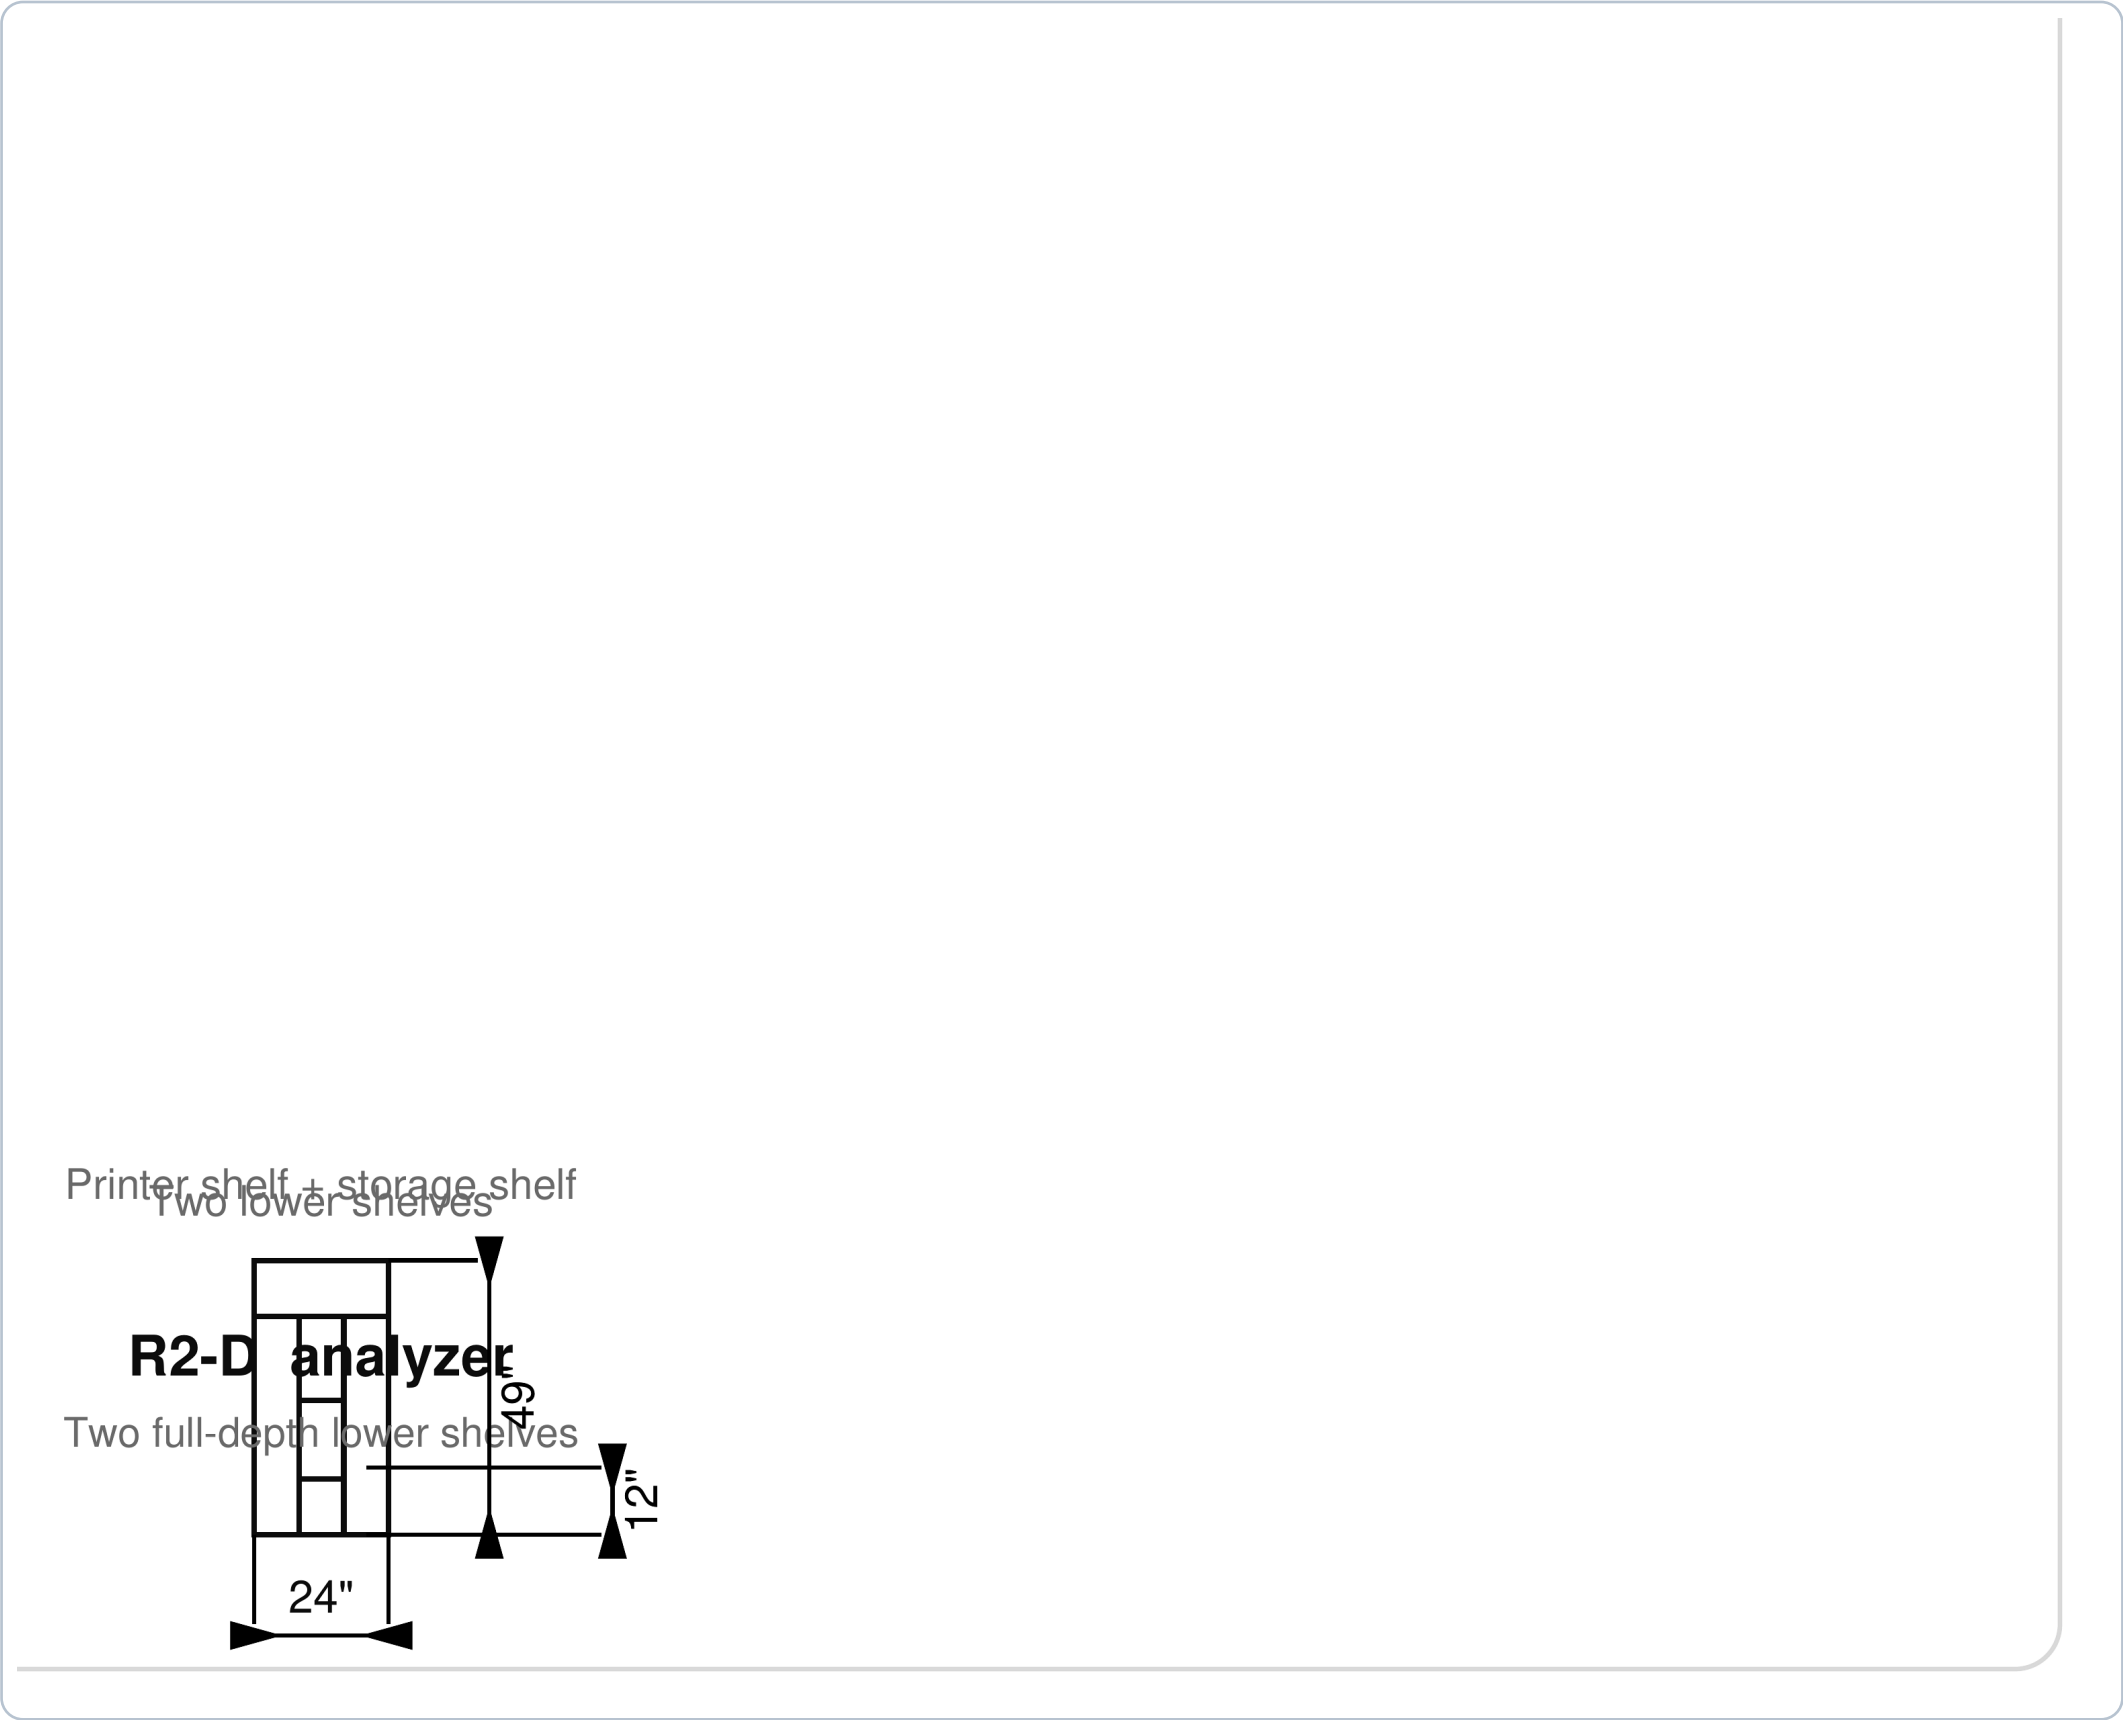

Detail 7 - Room 3 microscope bench elevation

Z-011

Two 70 in benches shown as 141 in overall

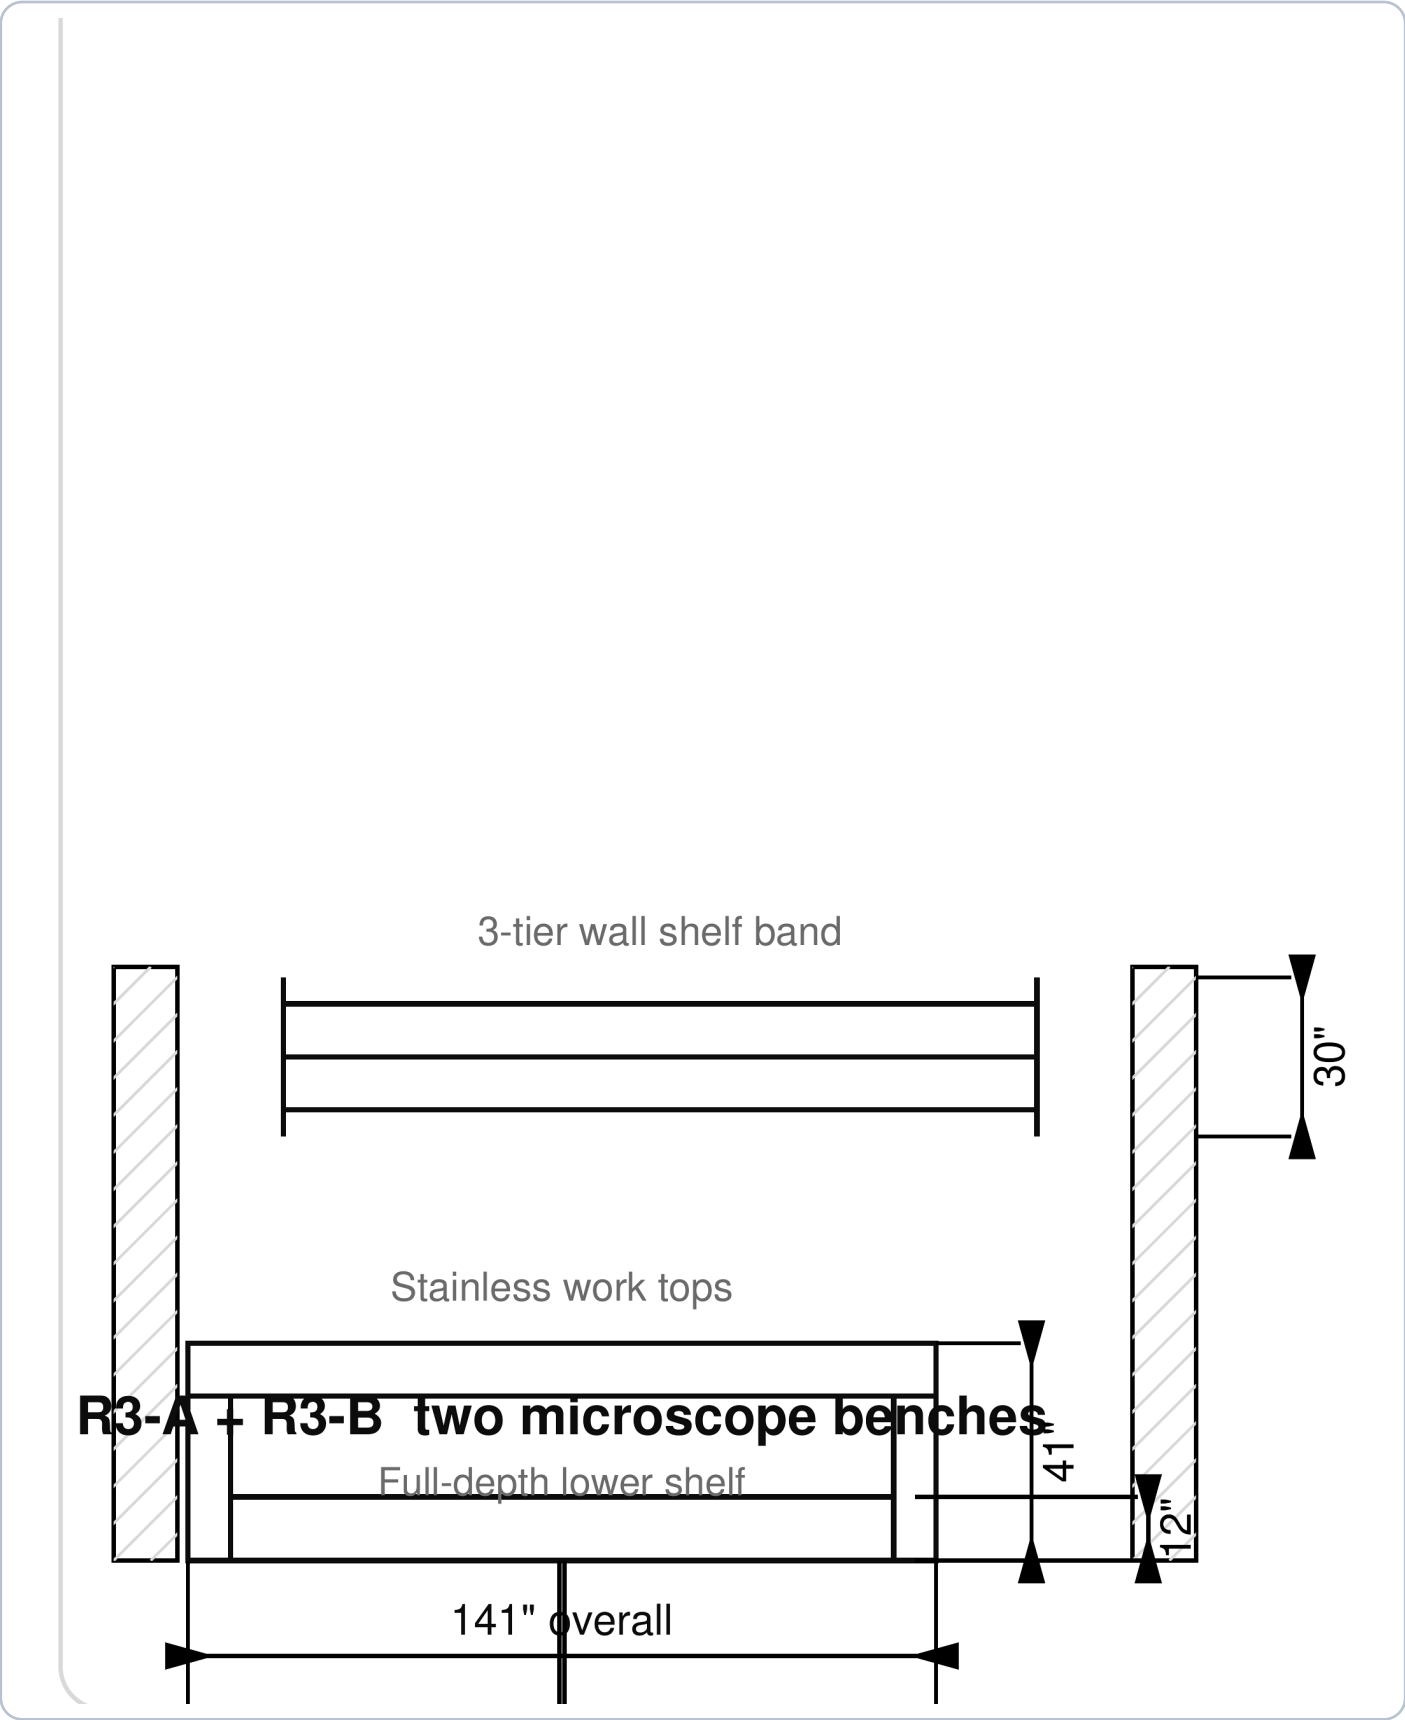


Detail 8 - Room 3 analyzer stand

Approx. 21 x 22 x 35

Z-012


Compact analyzer stand

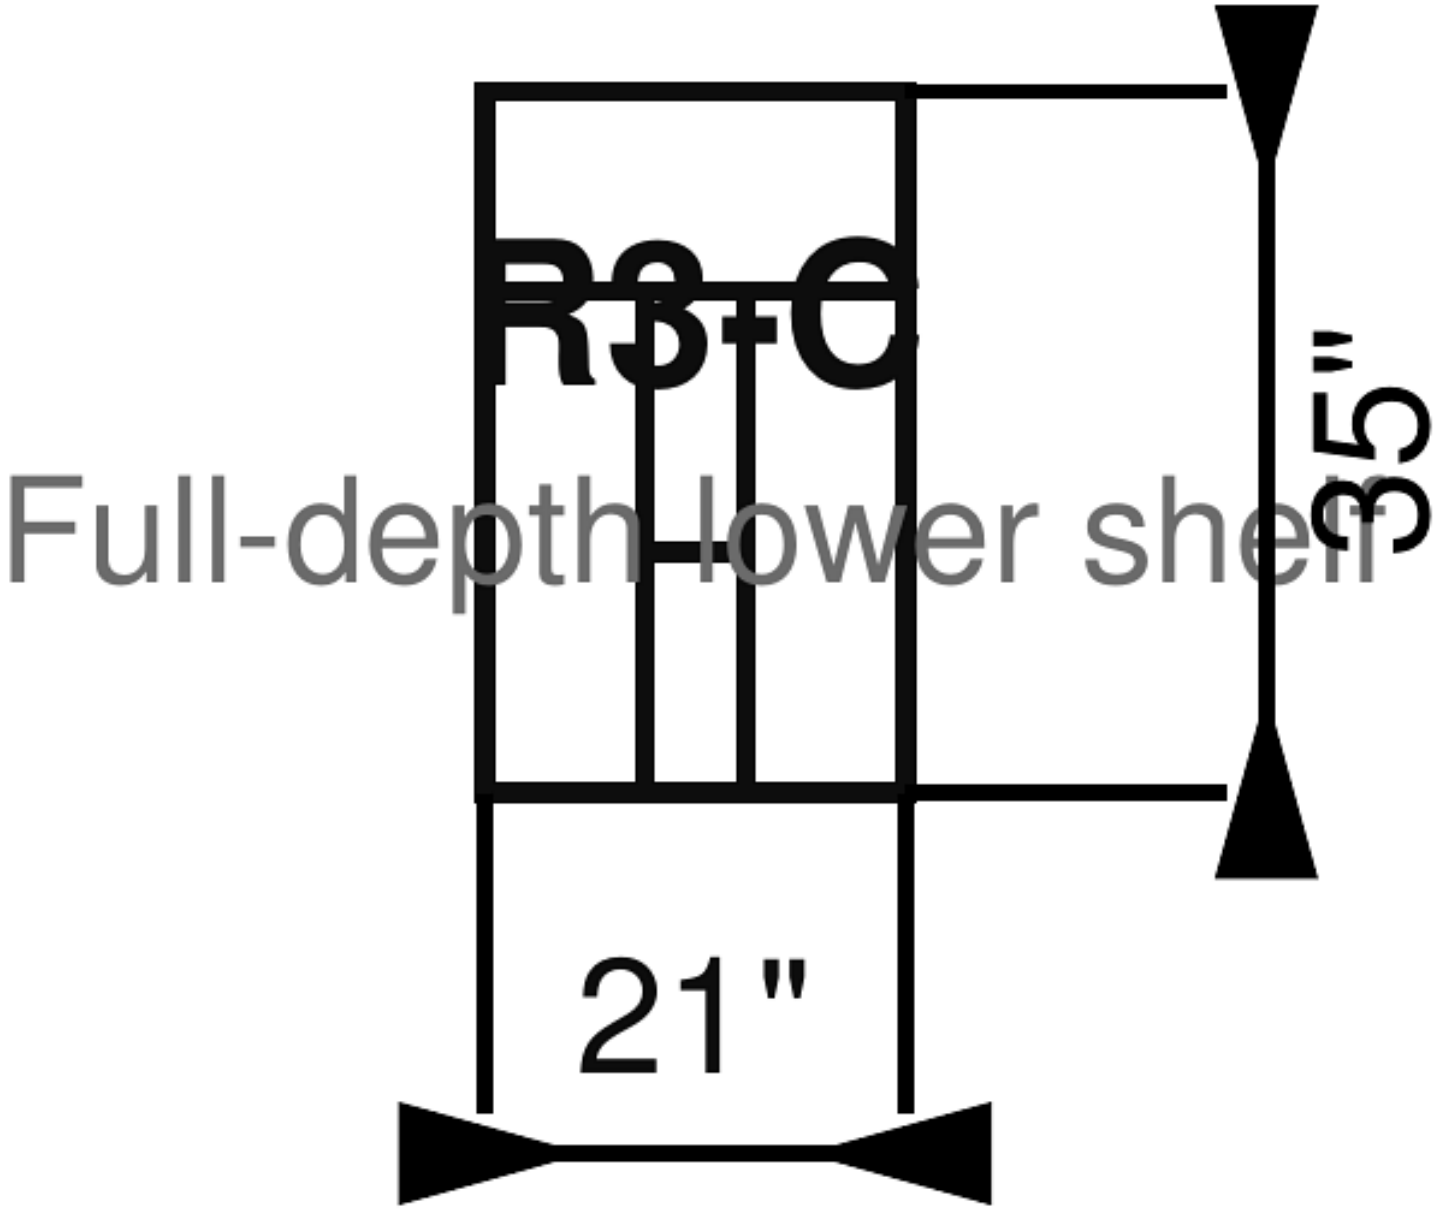

Detail 9 - Room 4 workstation elevation

Z-013

Approx. 72 x 30 x 41 with wall shelf above

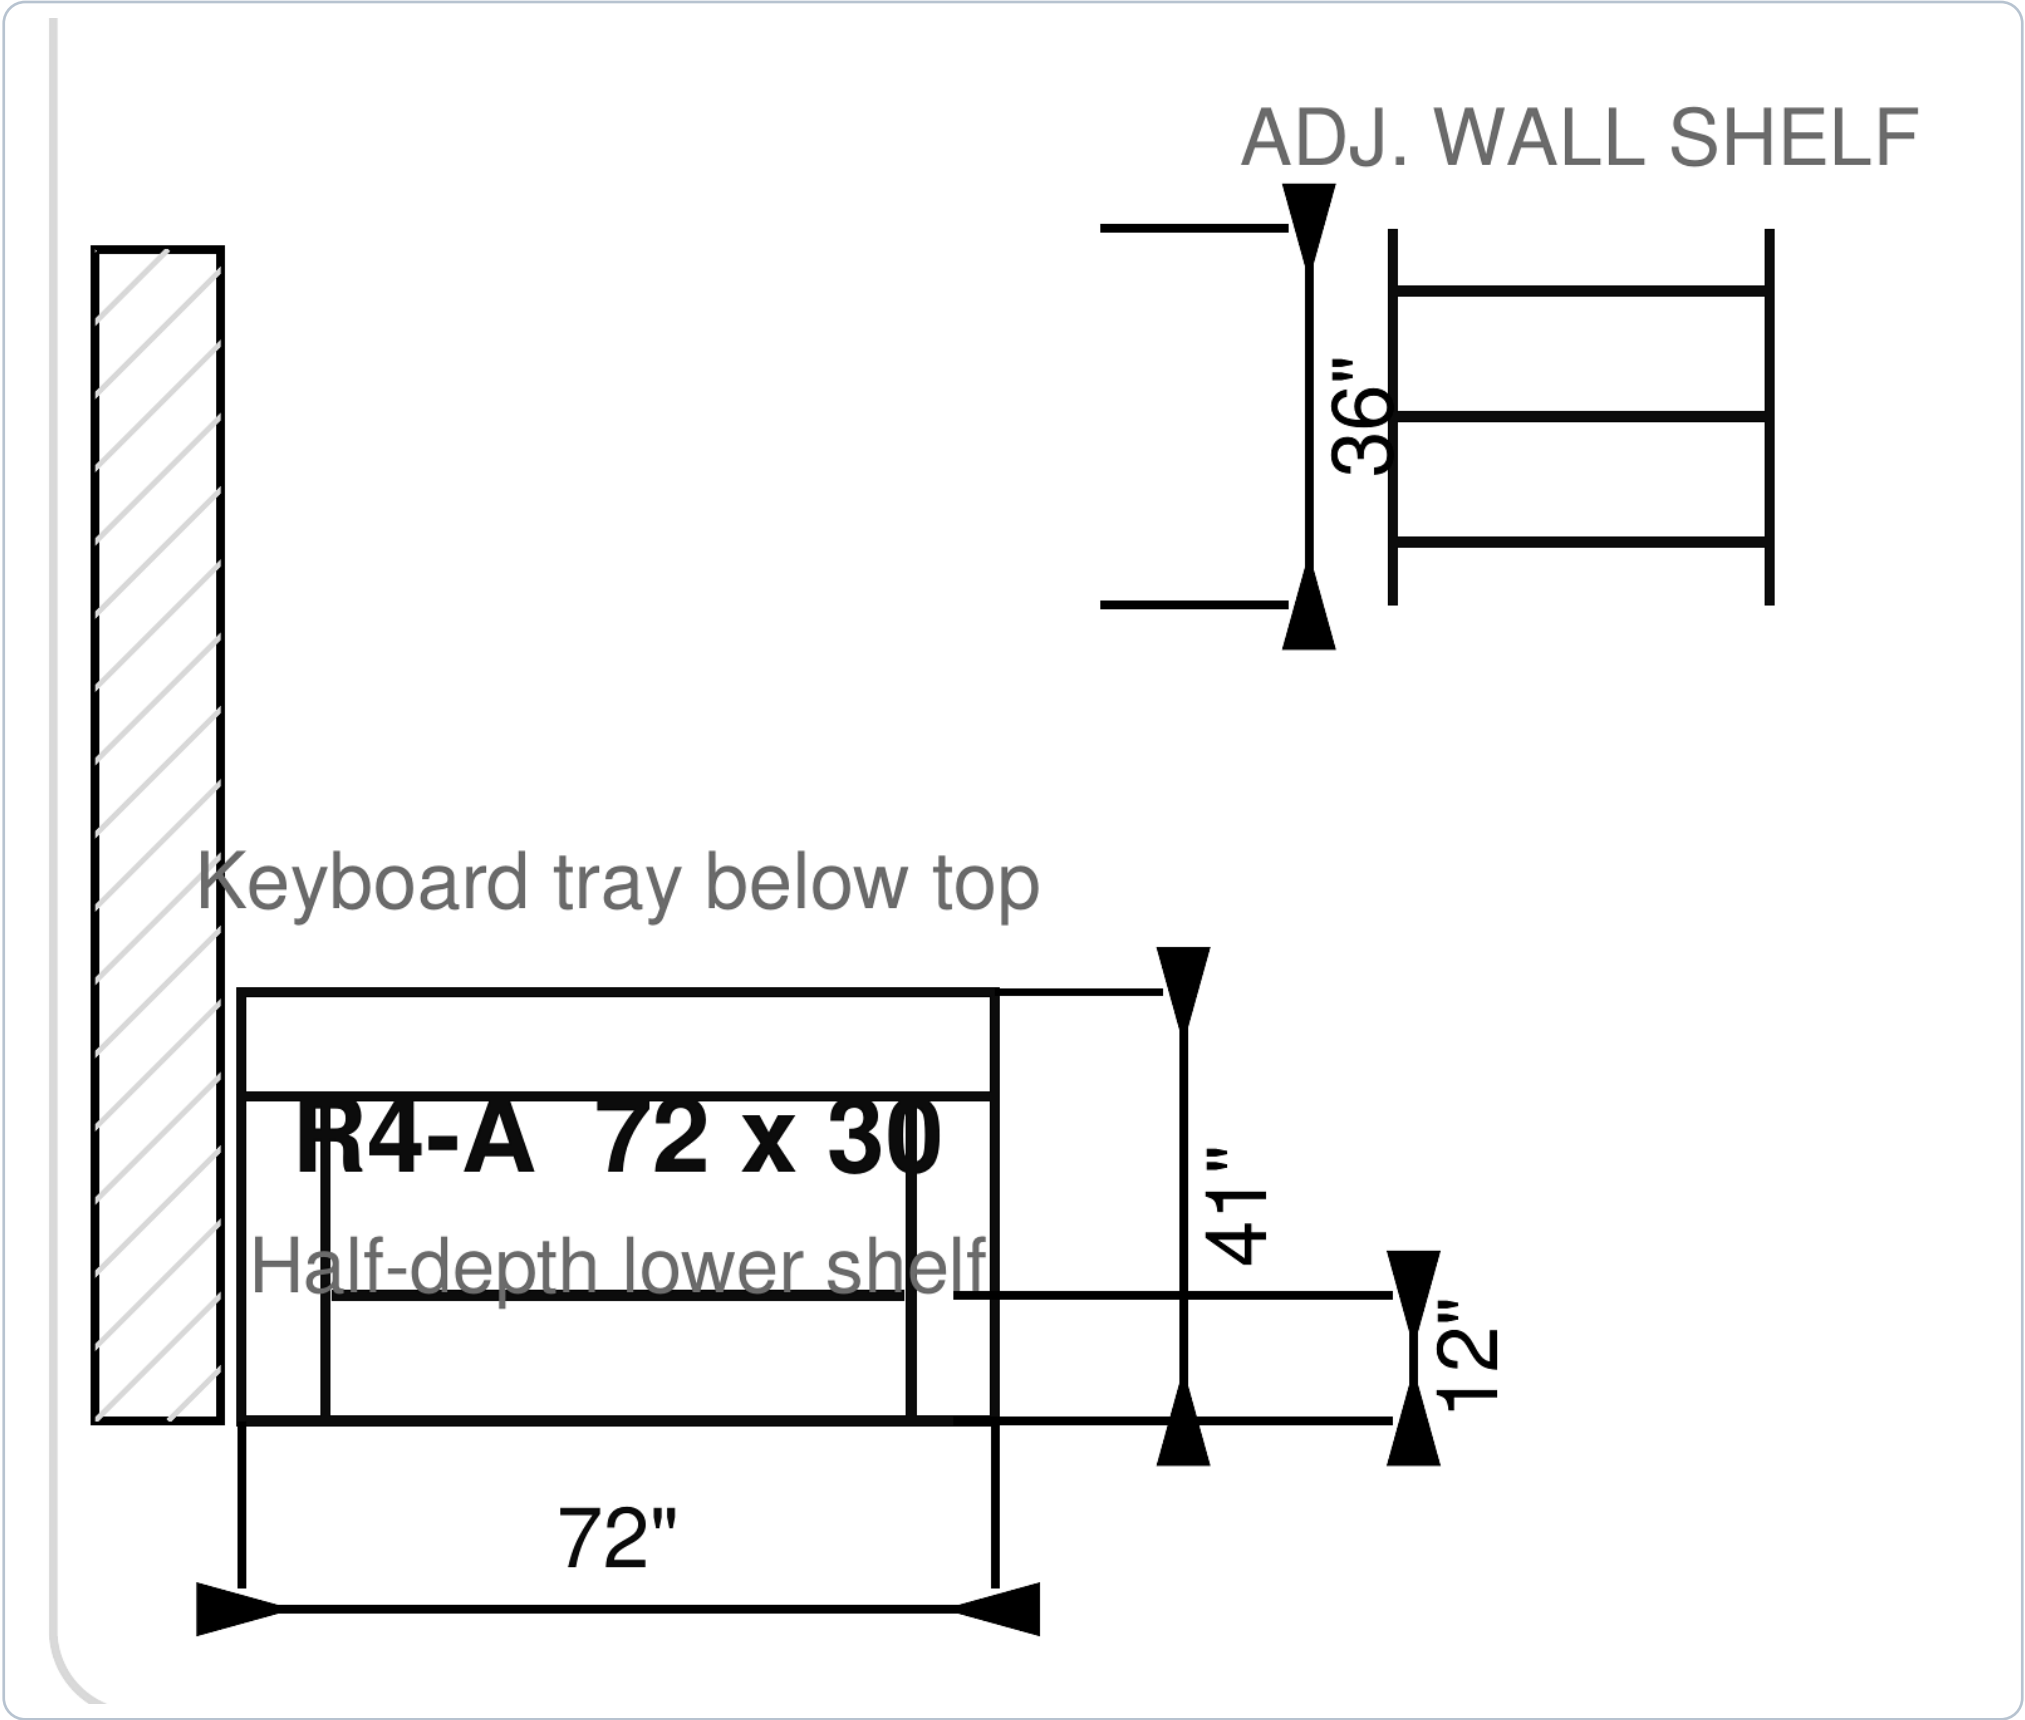

Detail 10 - Room 4 analyzer table elevation

Z-014

Approx. 32 x 36 x 41 with keyboard tray

