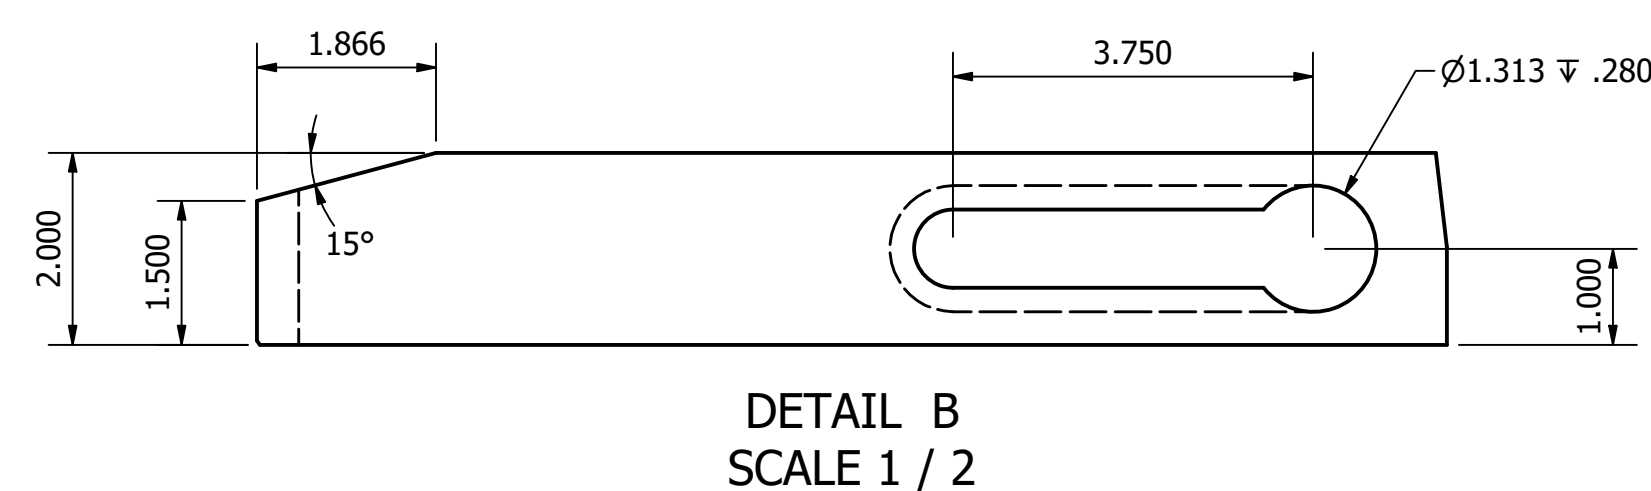
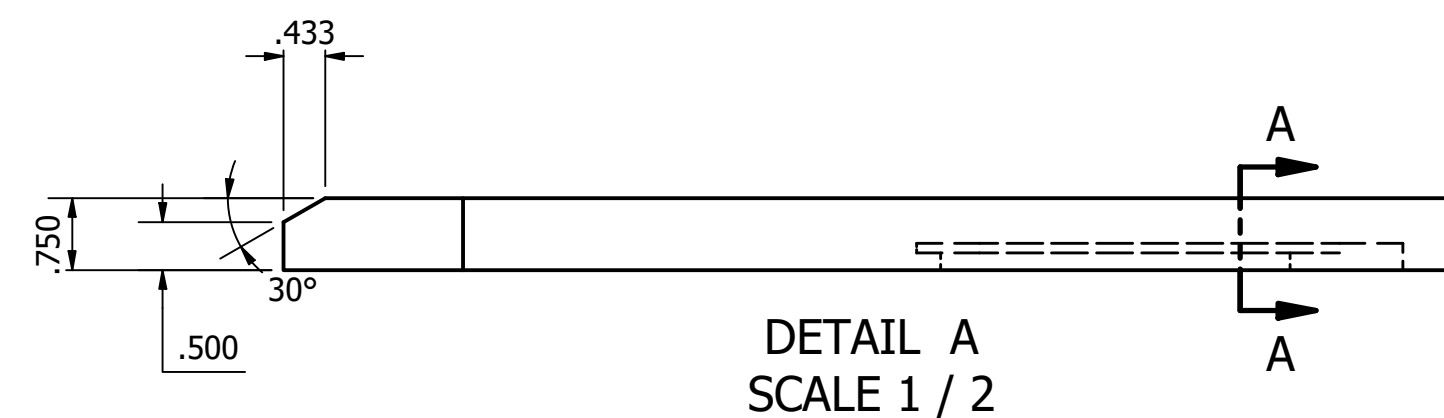
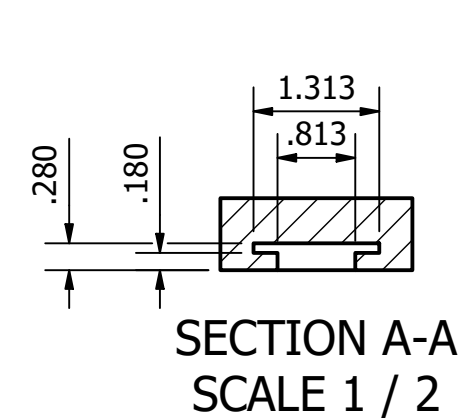
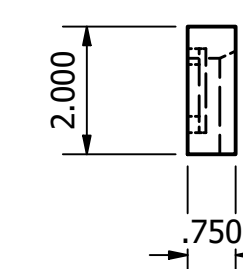
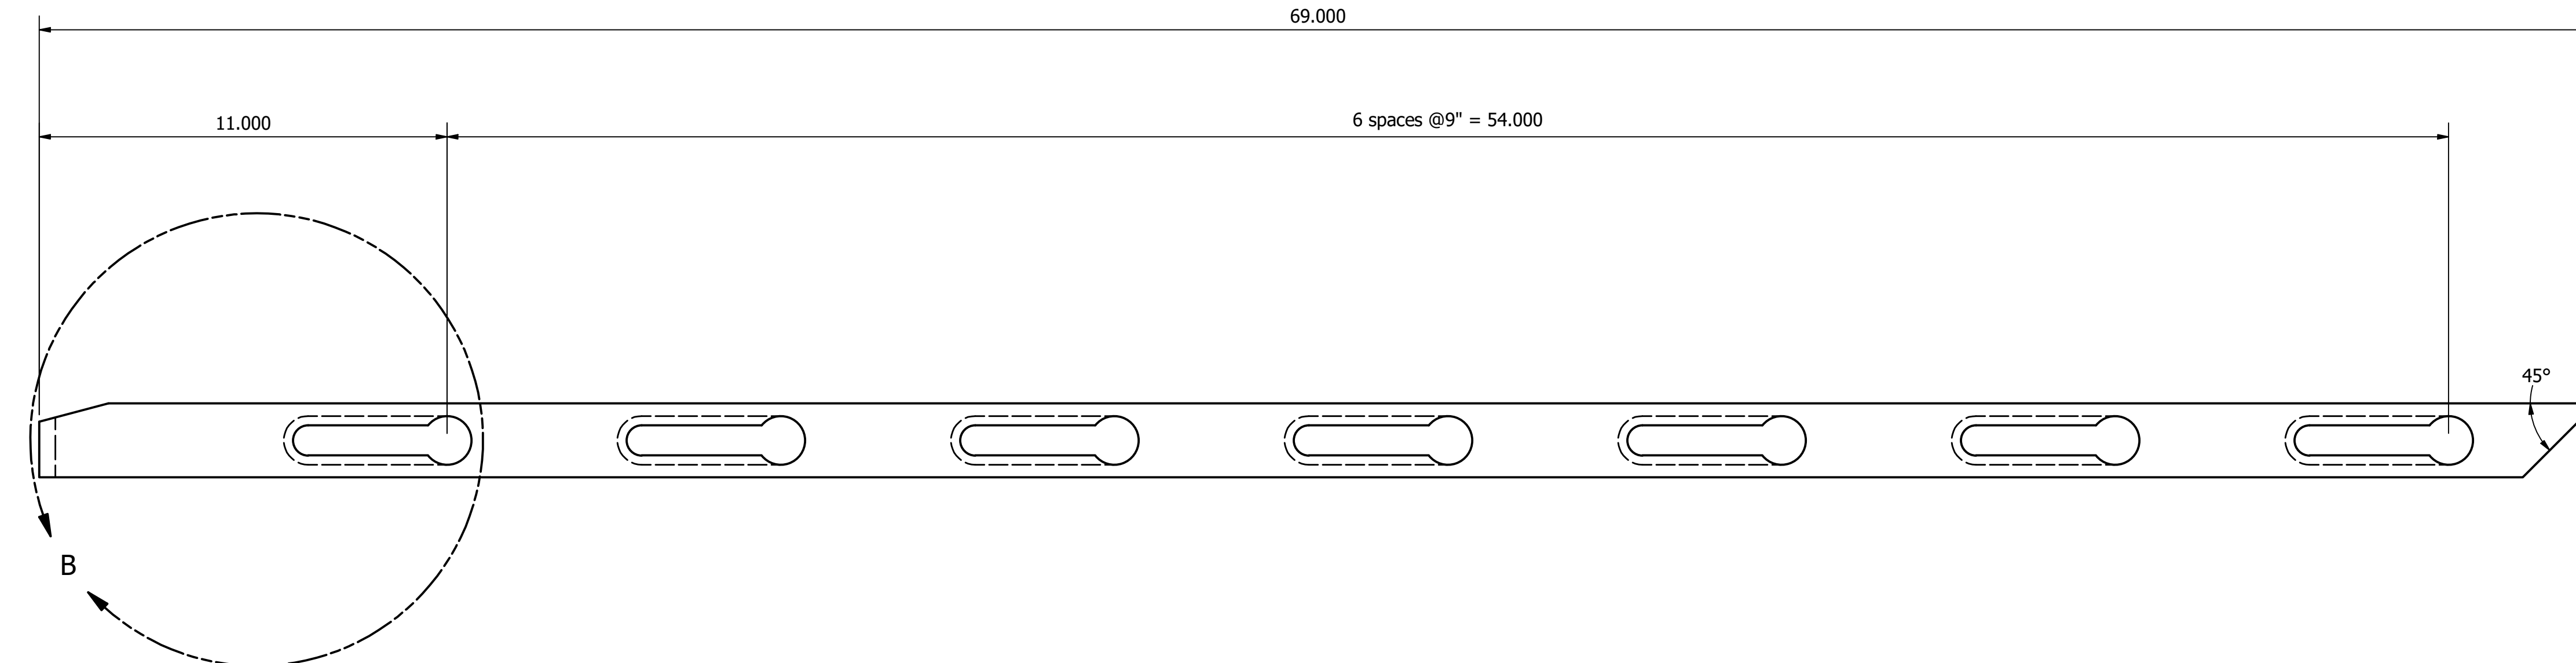
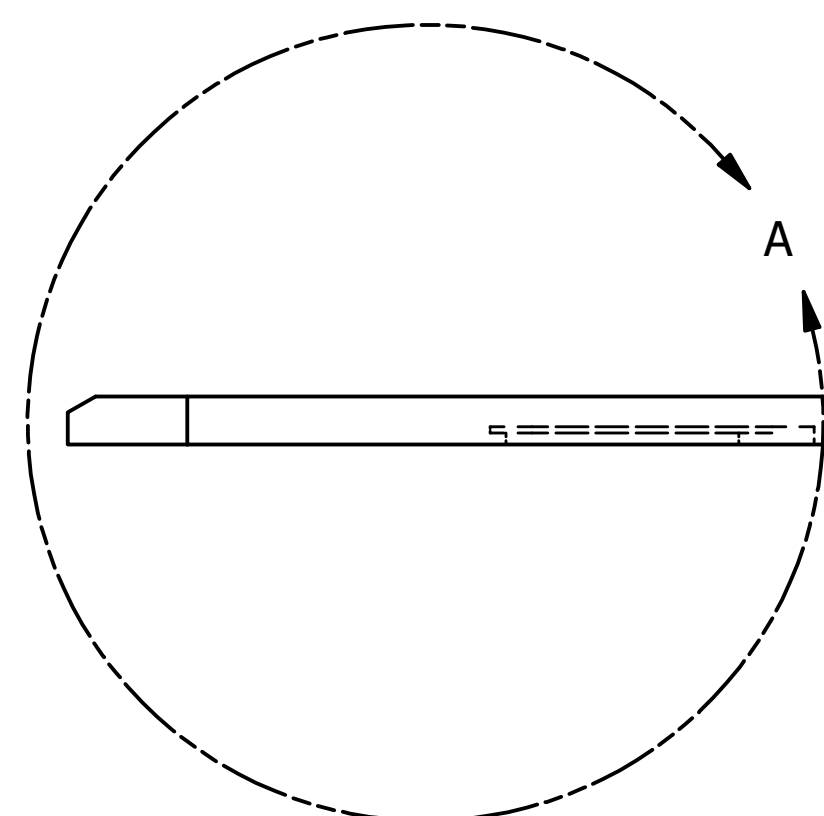


[illegible]

U.S. ARMY CORPS OF ENGINEERS PORTLAND DISTRICT	DESIGNED BY: ADRIAN MARSHALL ABLELAND	DATE:
	DWN BY: GOODAMM	SOLICITATION NO.:
JOHN DAY ENGINEERING RUFUS, OR	SUBMITTED BY:	CONTRACT NO.:
	PILOT SCALE:	PILOT DATE:
	SIZE:	DRAWING NUMBER:
	FILE NAME:	

COLUMBIA RIVER, WA
JOHN DAY LOCK AND DAM
SUBMERGED TRAVELING SCREENS

REPLACEABLE TRACK ASSEMBLY
25-3 REPLACEABLE TRACK (1)
BOTTOM SECTION


SHEET
IDENTIFICATION
M-101

DATE PLOTTED: 12/5/2025

USERNAME:	G20DJAAAM
-----------	-----------

SHEET NAME:

DESIGN FILE: M:\Engineering Staff\Mariscal Arellano\013_FY25\003_STS New Start Documents\Replaceable Tracks\2nd Design\Replaceable Tracks.dwg




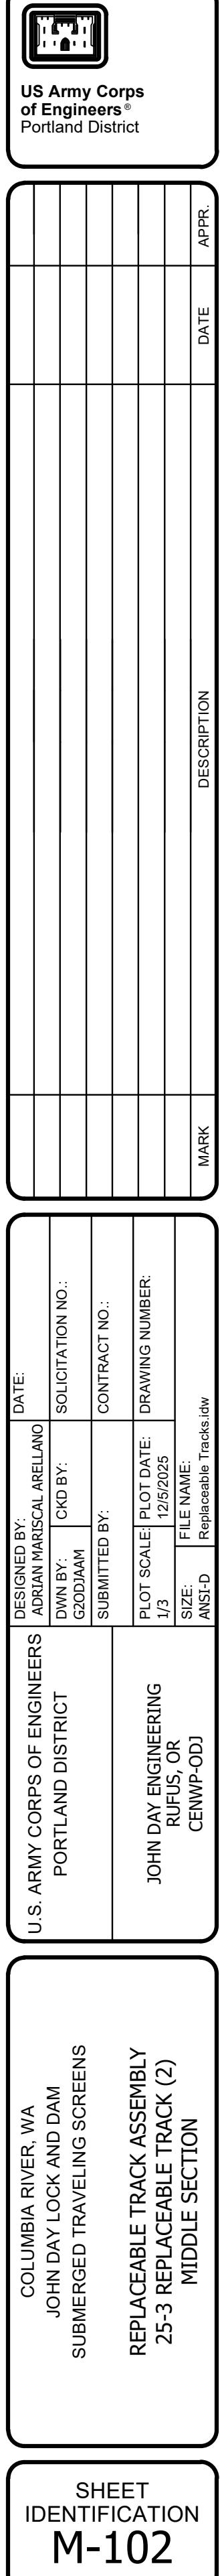


[illegible][illegible]


COLOMBIA RIVERS, WA
JOHN DAY LOCK AND DAM
SUBMERGED TRAVELING SCREENS
REPLACEABLE TRACK ASSEMBLY
25-3 REPLACEABLE TRACK (3)
TOP SECTION

SHEET
IDENTIFICATION
M-103


DESIGN FILE: M:\Engineering\Staff\Mariscal Arellano\013. FY 25\003. S15 New Start Documents\Replaceable | racks\2nd Design\Replaceable | racks.idw

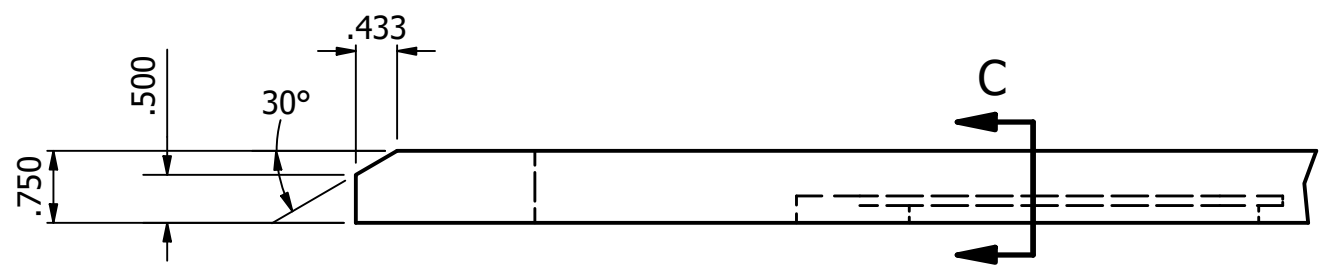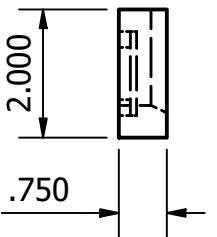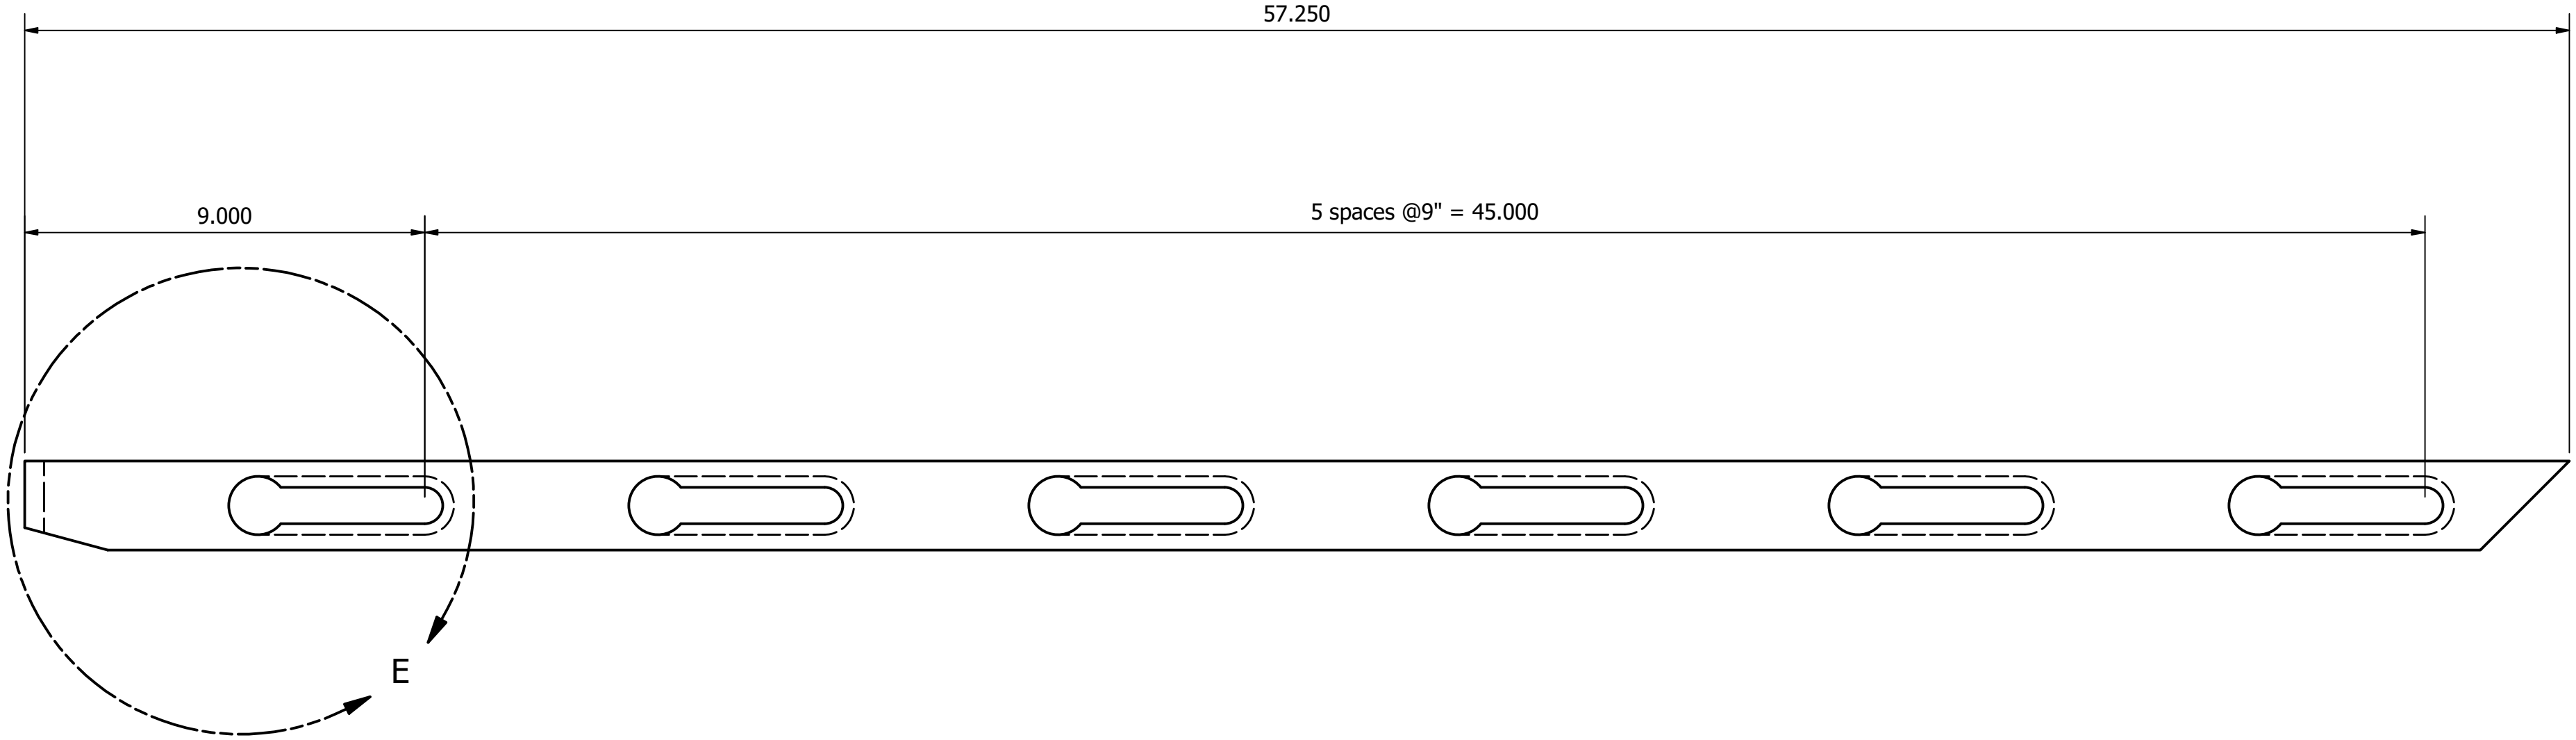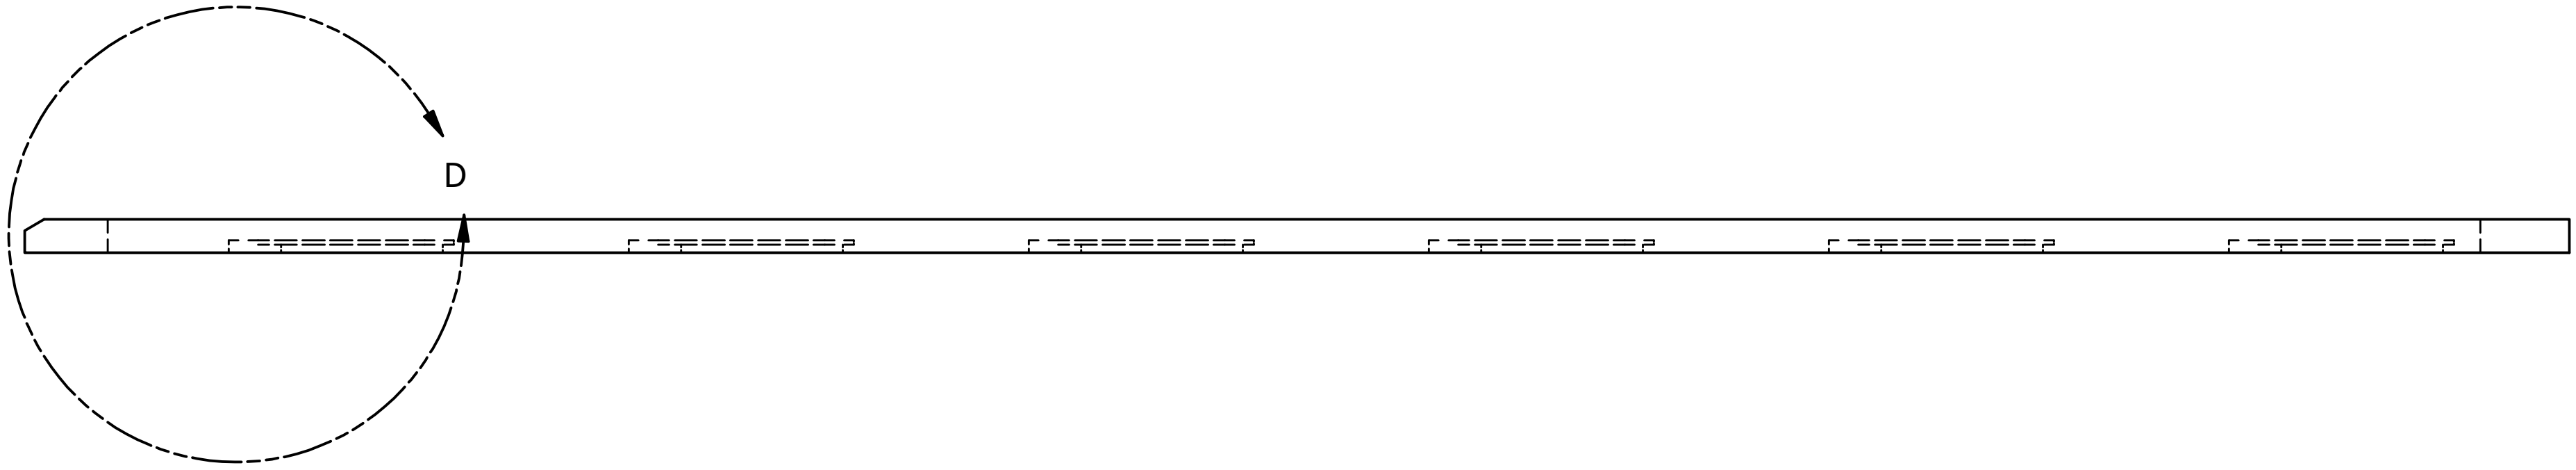



DETAIL D
SCALE 1 / 2

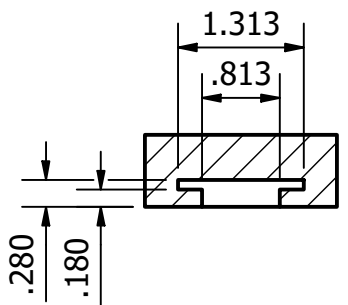


SECTION C-C
SCALE 1 / 2

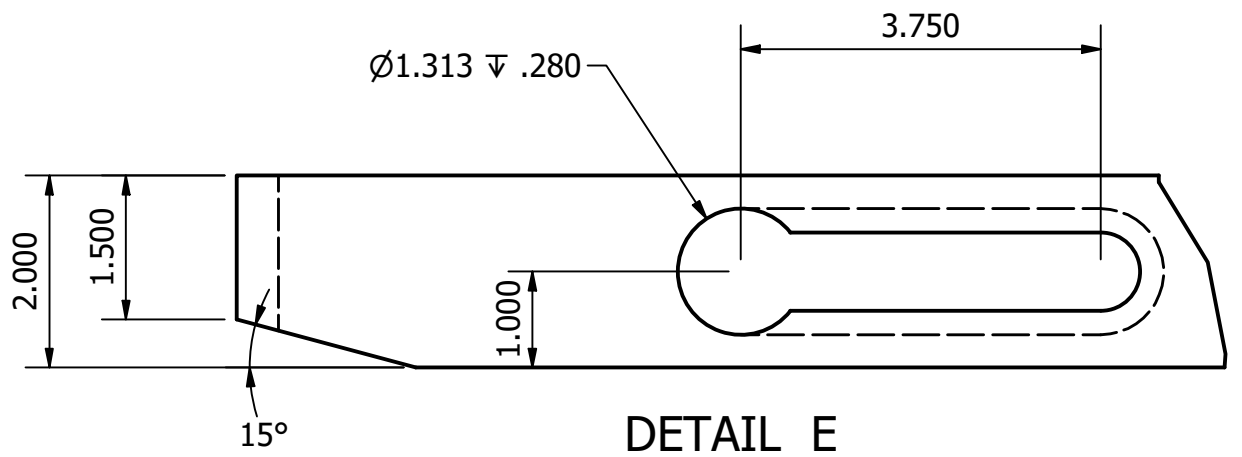



DETAIL E
SCALE 1 / 2

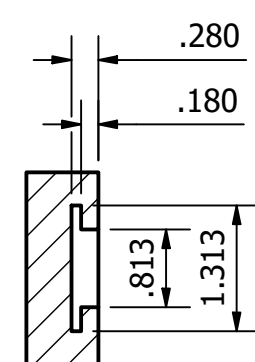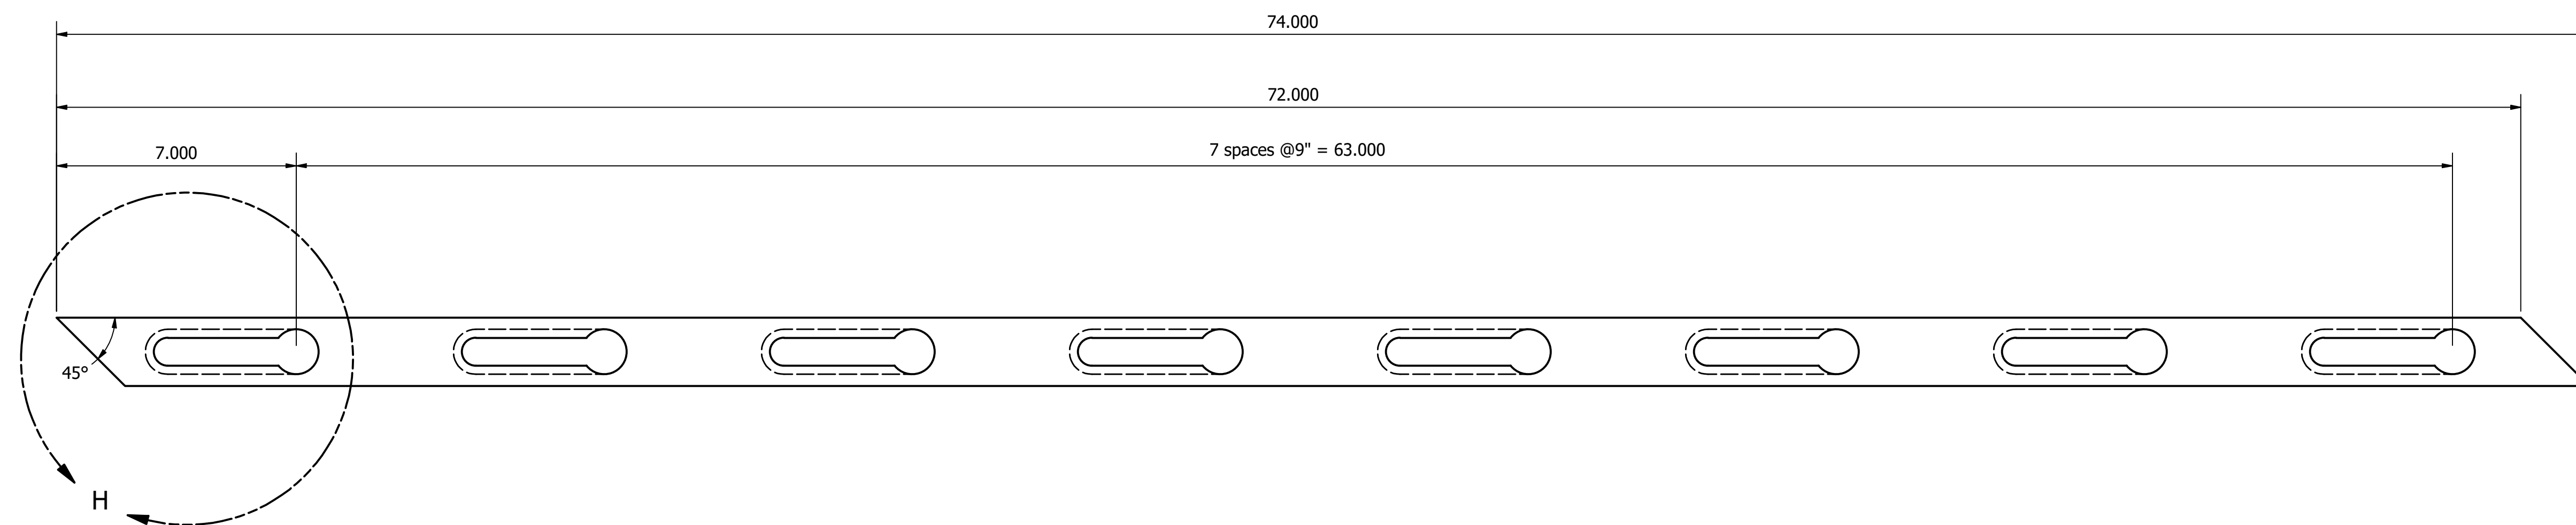

SECTION E-E
SCALE 1 / 2

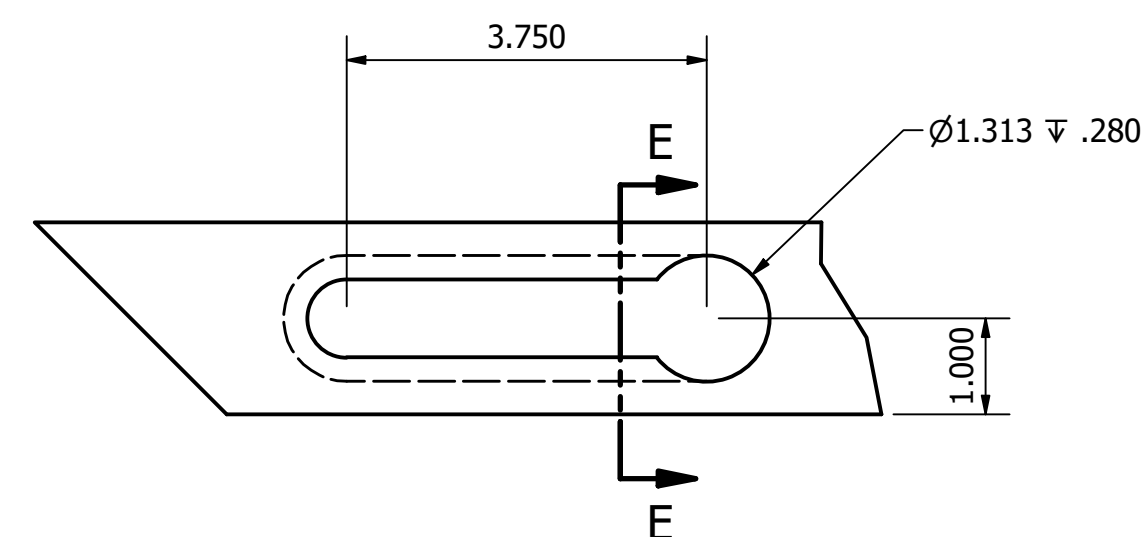

DETAIL H
SCALE 1 / 2

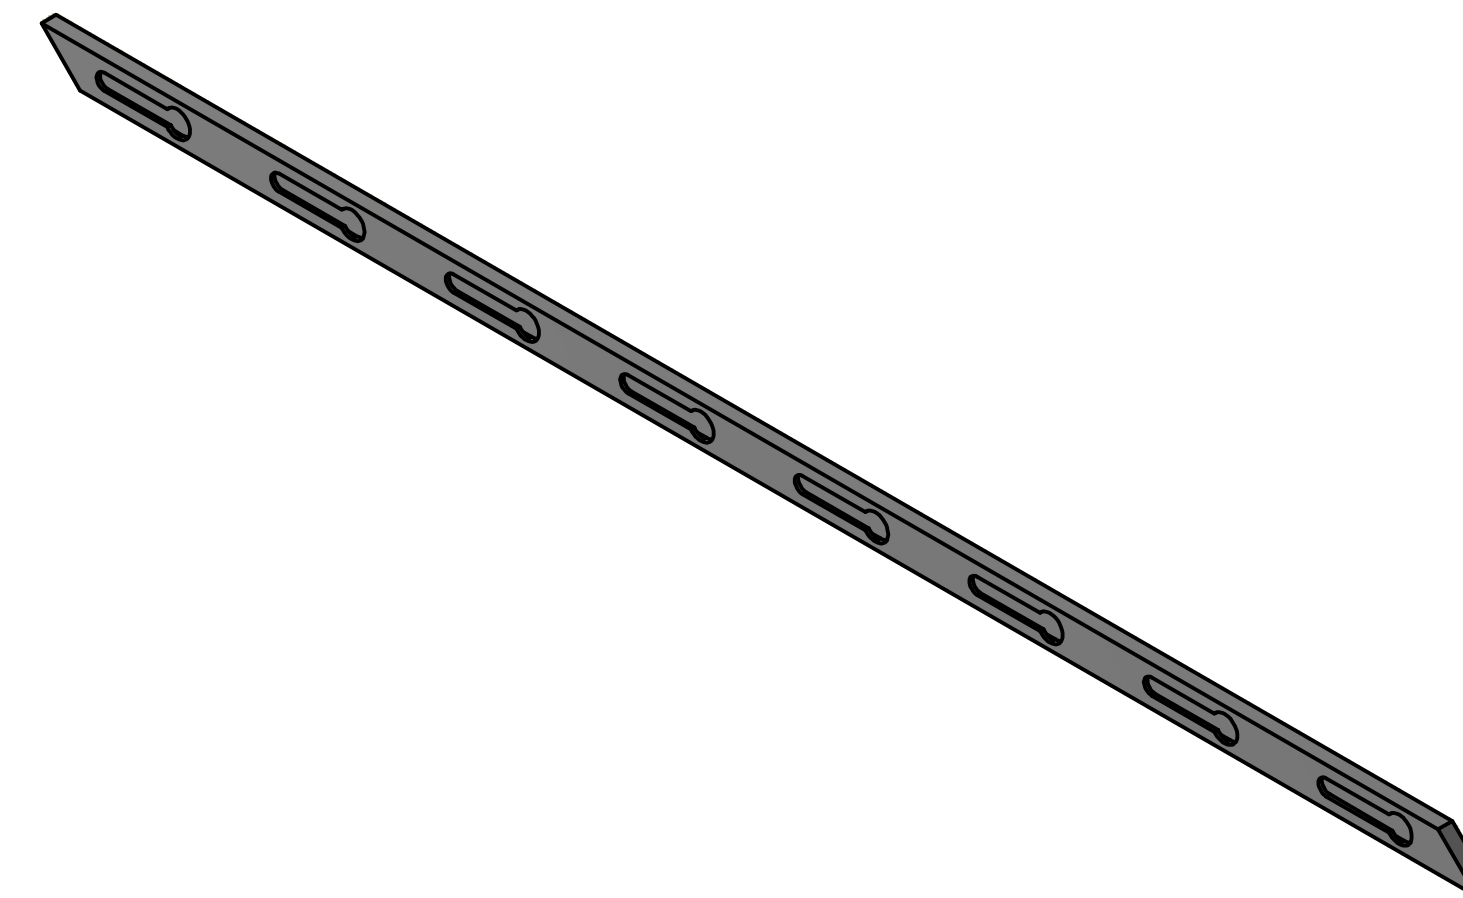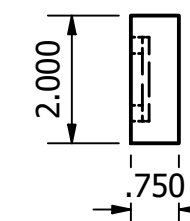

**US Army Corps
of Engineers®**
Portland District

[illegible]

U.S. ARMY CORPS OF ENGINEERS PORTLAND DISTRICT	DESIGNED BY: TECHNICAL AID/AND		DATE:
	DRAWN BY: GODDARD	CHECKED BY:	SOLICITATION NO:
JOHN DAY ENGINEERING RUFUS, OR	SUBMITTED BY:		CONTRACT NO.:
	PLOT SCALE: 1/13		PLOT DATE: 12/26/02
		DRAWING NUMBER	
		SIZE: FILE NAME:	

COLUMBIA RIVER, WA
JOHN DAY LOCK AND DAM
SUBMERGED TRAVELING SCREENS

REPLACEABLE TRACK ASSEMBLY
25-4 REPLACEABLE TRACK (5)
MIDDLE SECTION

SHEET
IDENTIFICATION
M-105




DATE PLOTTED: 12/5/2025

USERNAME:	G2ODJAAM
-----------	----------


SHEET NAME:

DESIGN FILE: M:\Engineering\Staff\Mariscal Arellano\013. FY25\003. STS New Start Documents\Replaceable Tracks\2nd Design\Replaceable Tracks.rdw

A

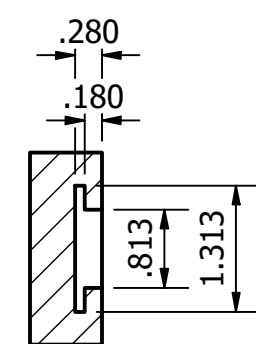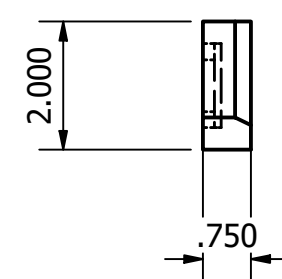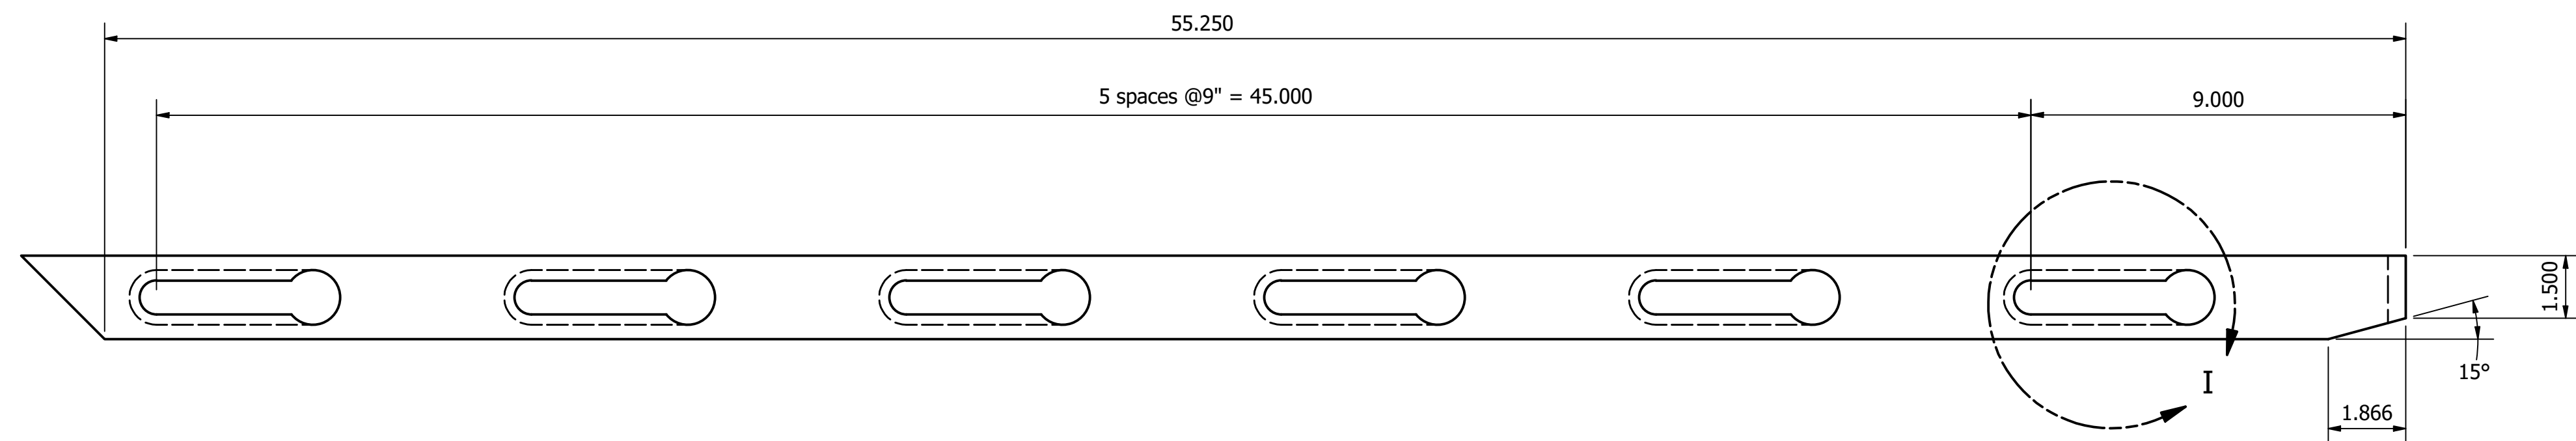

DETAIL I
SCALE 1 / 2

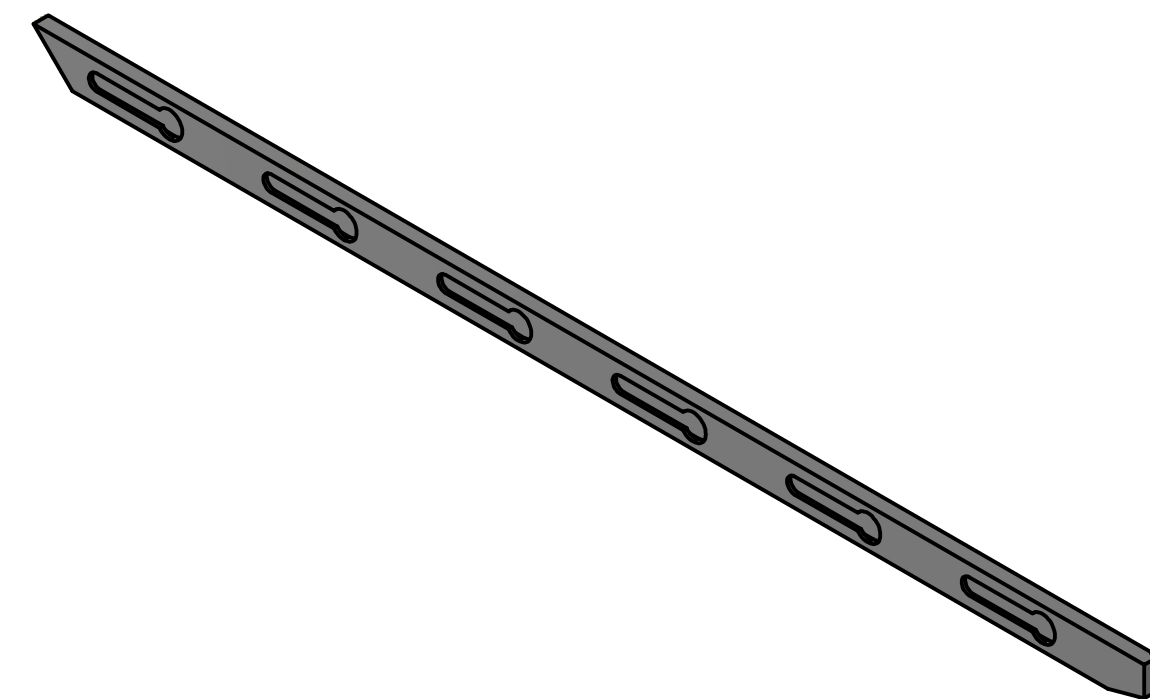[illegible]

U.S. ARMY CORPS OF ENGINEERS PORTLAND DISTRICT	DESIGNED BY:	DATE:
	DRAWN BY:	SOLICITATION NO.:
	CHECKED BY:	CONTRACT NO.:
	SUBMITTED BY:	DRAWING NUMBER:
JOHN DAY ENGINEERING RUFUS OR CENWP-001	PLOT SCALE:	PLOT DATE:
	1/3	12/5/2025
	FILE NAME:	

COLUMBIA RIVER, WA
JOHN DAY LOCK AND DAM
SUBMERGED TRAVELING SCREENS
REPLACEABLE TRACK ASSEMBLY
25-4 REPLACEABLE TRACK (6)

SHEET
IDENTIFICATION
M-106

SHEET NAME:

DESIGN FILE: M:\Engineering\Staff\Mariscal Arellano\013. FY25\003. STS New Start Documents\Replaceable Tracks\2nd Design\Replaceable Tracks.dwg