

US DEPARTMENT OF VETERAN AFFAIRS
CHILLICOTE VA MEDICAL CENTER
17273 STATE ROUTE 104
CHILLICOTHE, OH 45601-9715

VA CHILLICOTHE (EHRM) ELECTRONIC HEALTH RECORDS
MODERNIZATION INFRASTRUCTURE UPGRADES

VA PROJECT NUMBER: 538-21-705

VA CONTRACT NUMBER: 36C77623C0079

100% CONSTRUCTION DOCUMENT

DATE 10/20/2025



Autobest Docs:223-011 VA Chilliloth EHRM 1223-011 VA Chilliloth Arch Model, Bldg 018.rvt

10% BASIS OF DESIGN	09/27/2023
35% SCHEMATIC DESIGN	10/27/2023
65% DESIGN DEVELOPMENT	04/07/2025
95% CONSTRUCTION DOCUMENTS	06/12/2025
95% CONSTRUCTION DOCUMENTS - REV 1	09/15/2025
100% CONSTRUCTION DOCUMENTS	10/20/2025
Revisions:	Date

CONSULTANT

CONSULTANT:

ARCHITECT/ENGINEER OF RECORD

A/E:
GDM-AE, Inc.
1308 NE 134th St, SUITE A
VANCOUVER, WA 98685
P: 541.436.4723
WWW.GDM-AE.COM
CELYN DEZMAIN

GDM
ARCHITECTS • ENGINEERS

STAMP



VA

STATION
538

U.S. Department
of Veterans Affairs

DRAWING TITLE

COVER SHEET

APPROVED:

RYAN JETER
FOR OFFICIAL USE ONLY (FOUO)
NOT FOR CONSTRUCTION

PHASE

100% CONSTRUCTION
DOCUMENT

FLS

**FULLY
SPRINKLERED**

PROJECT TITLE

VA CHILLICOTHE (EHRM) ELECTRONIC
HEALTH RECORDS MODERNIZATION
INFRASTRUCTURE UPGRADES

LOCATION

17273 STATE ROUTE 104
CHILLICOTHE, OH 45601-9715

ISSUE DATE

10/20/2025

CHECKED BY

CD

DRAWN BY

MA

PROJECT NO.

538-21-705

BUILDING NO.

18

DRAWING NO.

G-001

APPLICABLE CODES, REGULATIONS AND DESIGN MANUALS

APPLICABLE CODES, STANDARDS, VA DESIGN MANUALS AND DIRECTIVES

VA OFFICE OF ELECTRONIC HEALTH RECORD MODERNIZATION OEHRM SITE INFRASTRUCTURE AND ENDER USER DEVICE (EUD) REQUIREMENTS APRIL 15, 2021 (VERSION 2.0 CONCURRENT) PARAGRAPH 2.9 PHYSICAL SECURITY DESIGN REQUIREMENTS STATES:
TELECOMMUNICATIONS ROOMS (TRS) AND DATA CENTERS SHALL COMPLY WITH THE FOLLOWING DESIGN MANUALS AND EHRM PROGRAM REQUIREMENTS:
U.S. DEPARTMENT OF VETERANS AFFAIRS OFFICE OF CONSTRUCTION & FACILITIES MANAGEMENT TELECOMMUNICATIONS AND SPECIAL TELECOMMUNICATIONS SYSTEMS DESIGN MANUAL, FEBRUARY 2016 (PG-18-12) [HTTPS://WWW.CFM.VA.GOV/TL/DCGUIDE.ASAP](https://www.cfm.va.gov/tl/DCGUIDE.ASAP)
U.S. DEPARTMENT OF VETERANS AFFAIRS OFFICE OF INFORMATION & TECHNOLOGY (OIT) INFRASTRUCTURE STANDARDS FOR TELECOMMUNICATIONS SPACES VERSION 3.1 1 JULY 2021
OIT DESIGN GUIDE TEMPLATES FOR CRITICAL INFRASTRUCTURE IN TELECOMMUNICATIONS SPACES (CLINICAL AND NON-CLINICAL ENVIRONMENTS), APRIL 16, 2020
VA PHYSICAL SECURITY AND RESILIENCY DESIGN MANUAL, REV APRIL 1, 2021
ANSI/TIA-642-B TELECOMMUNICATIONS INFRASTRUCTURE STANDARD FOR DATA CENTERS
VA HANDBOOK APPENDIX B 07304 PHYSICAL SECURITY REQUIREMENTS SECURITY AND LAW ENFORCEMENT APPENDIX B PHYSICAL SECURITY REQUIREMENTS FOR IT DATA CENTERS AND SEVER ROOMS, DECEMBER 12, 2012.

ACCESSIBILITY CODE

FEDERAL ARCHITECTURAL BARRIERS ACT ACCESSIBILITY STANDARDS (ABAAAS), REV 2015
PG-18-13 VA FIRE BARRIER (A SUPPLEMENT TO FEDERAL BARRIERS ACT ACCESSIBILITY STANDARDS) FIRE DESIGN GUIDE, DEC 2011

BUILDING CODES

2021 INTERNATIONAL BUILDING CODE (IBC) WHERE NFPA 101 AND ASSOCIATED DOCUMENTS ARE SILENT
2021 INTERNATIONAL ENERGY CONSERVATION CODE
2021 INTERNATIONAL FIRE CODE (IFC), WHERE NFPA STANDARDS AND CODES ARE SILENT

NATIONAL FIRE PROTECTION ASSOCIATION (NFPA)

NFPA 1: FIRE CODE, 2021
NFPA 10: STANDARD FOR PORTABLE FIRE EXTINGUISHERS, 2022
NFPA 13: STANDARD FOR THE INSTALLATION OF SPRINKLER SYSTEMS, 2022
NFPA 30: FLAMMABLE AND COMBUSTIBLE LIQUIDS CODE, 2021
NFPA 70: NATIONAL ELECTRICAL CODE, 2020
NFPA 70E: STANDARD FOR ELECTRICAL SAFETY IN THE WORKPLACE, 2021
NFPA 72: NATIONAL FIRE ALARM AND SIGNALING CODE, 2022
NFPA 75: STANDARD FOR THE FIRE PROTECTION OF INFORMATION TECHNOLOGY EQUIPMENT, 2020
NFPA 101: LIFE SAFETY CODE, 2021
NFPA 241: STANDARD FOR SAFEGUARDING CONSTRUCTION, ALTERATION, AND DEMOLITION OPERATIONS, 2022
NFPA 281: RECOMMENDED PRACTICE FOR WATER FLOW TESTING AND MARKING OF HYDRANTS, 2022
NFPA 2001: STANDARD ON CLEAN AGENT FIRE EXTINGUISHING SYSTEMS 2022

VA DESIGN MANUALS

VA OFFICE OF CONSTRUCTION AND FACILITY MANAGEMENT DESIGN MANUAL AUGUST 1, 2014
PG-18-1 MASTER CONSTRUCTION SPECIFICATIONS, [HTTP://WWW.CFM.VA.GOV/TL/DCGUIDE.ASAP](http://www.cfm.va.gov/tl/DCGUIDE.ASAP)
PG-18-3 DESIGN AND CONSTRUCTION PROCEDURES, APRIL 2019, [HTTP://WWW.CFM.VA.GOV/TL/CPRO.ASP](http://www.cfm.va.gov/tl/CPRO.ASP)
PG-18-14 ROOM FINISHES, DOOR AND HARDWARE SCHEDULE – DECEMBER 2018

U.S. DEPARTMENT OF VETERANS AFFAIRS OFFICE OF INFORMATION & TECHNOLOGY (OIT) INFRASTRUCTURE STANDARDS FOR TELECOMMUNICATIONS SPACES (ISTS) VERSION 4.0 JUNE 1, 2023

HVAC DESIGN MANUAL—NOVEMBER 1, 2017, REV MAY 1, 2019, REV 3/1/2020

VA ELECTRICAL DESIGN MANUAL – DECEMBER 1, 2019

VA FIRE PROTECTION DESIGN MANUAL, NINTH EDITION, NOVEMBER 1ST, 2023

LIGHTING DESIGN MANUAL — DECEMBER 2015 [HTTP://WWW.CFM.VA.GOV/TL/DCMANUAL/DMLIGHTING.PDF](http://www.cfm.va.gov/tl/DCMANUAL/DMLIGHTING.PDF)

VA SEISMIC CODES AND STANDARDS, H-18-8 [HTTP://WWW.CFM.VA.GOV/TL/SEISMIC.ASP](http://www.cfm.va.gov/tl/SEISMIC.ASP)

SUSTAINABLE DESIGN MANUAL MANUAL – REV 1 AUGUST 18, 2017,

ASBESTOS ABATEMENT DESIGN MANUAL FOR NEW HOSPITALS, REPLACEMENT HOSPITALS, AMBULATORY CARE, CLINICAL ADDITIONS, ENERGY CENTERS, OUTPATIENT CLINICS, ANIMAL RESEARCH FACILITIES, LABORATORY BUILDINGS – JULY 2011

MECHANICAL DESIGN STANDARDS

AMERICAN SOCIETY OF HEATING, REFRIGERATION, AND AIR-CONDITIONING ENGINEERS (ASHRAE)
STANDARD 62.1 - VENTILATION FOR ACCEPTABLE INDOOR AIR QUALITY, 2017
STANDARD 90.1 - ENERGY STANDARD FOR BUILDINGS EXCEPT LOW-RISE RESIDENTIAL BUILDINGS, 2013
STANDARD 170 - VENTILATION OF HEALTH CARE FACILITIES, 2021
SHEET METAL AND AIR CONDITIONING CONTRACTORS NATIONAL ASSOCIATION
HVAC DUCT CONSTRUCTION STANDARDS - METAL AND FLEXIBLE
HVAC SYSTEMS COMMISSIONING MANUAL, 2ND EDITION, 2015
SEISMIC RESTRAINT MANUAL GUIDELINES FOR MECHANICAL SYSTEMS, 3RD EDITION, 2008
US DEPARTMENT OF VETERANS AFFAIRS (VA)
HVAC DESIGN MANUAL (REVISION 1), PG18-10, 1 MAY 2021
SUSTAINABLE DESIGN MANUAL (REVISION 1), 18 AUGUST 2017
A. REQUIREMENTS FOR VA MINOR NEW CONSTRUCTION AND RENOVATION PROJECTS (I.E. UNDER \$20,000,000) WHOLE BUILDING COMMISSIONING MANUAL (REVISION 1), NOVEMBER 2013

ELECTRICAL DESIGN STANDARDS

UNDERWRITER'S LABORATORY, INC (UL) STANDARDS – 2019
ANSI/TIA-568-D SERIES, COMMERCIAL BUILDING TELECOMMUNICATIONS CABLING STANDARD, AND ITS PUBLISHED ADDENDA -2017
ANSI/TIA 568-D-E, GENERIC TELECOMMUNICATIONS CABLING FOR CUSTOMER PREMISES, AND ITS PUBLISHED ADDENDA - 2017
ANSI/TIA 568 1-E, COMMERCIAL BUILDING TELECOMMUNICATIONS CABLING STANDARD, AND ITS PUBLISHED ADDENDA - 2017
ANSI/TIA 568 2-D, BALANCED TWISTED-PAIR TELECOMMUNICATIONS CABLING AND COMPONENTS. 2017
ANSI/TIA 568 3-D, OPTICAL FIBER CABLING COMPONENTS STANDARD, AND ITS PUBLISHED ADDENDA - 2017
ANSI/TIA 568 4-D BROADBAND COAXIAL CABLING AND COMPONENTS STANDARD
ANSI/TIA-569-C, COMMERCIAL BUILDING STANDARD FOR TELECOMMUNICATIONS PATHWAYS AND SPACES, AND ITS PUBLISHED ADDENDA - 2017
ANSI/TIA-606-A, ADMINISTRATION STANDARD FOR THE TELECOMMUNICATIONS INFRASTRUCTURE OF COMMERCIAL BUILDINGS, AND ITS PUBLISHED ADDENDA – 2017
ANSI/STD-607-A, COMMERCIAL BUILDING GROUNDING (EARTHING) AND BONDING REQUIREMENTS FOR TELECOMMUNICATIONS, AND ITS PUBLISHED ADDENDA – 2017
BUILDING INDUSTRIES CONSULTING SERVICES INTERNATIONAL (BICSI) – 2019
TELECOMMUNICATIONS DISTRIBUTION METHODS MANUAL (TDMM) -2020
NFPA 70E, 2021

STRUCTURAL ENGINEERING DESIGN STANDARDS

AMERICAN CONCRETE INSTITUTE (ACI 2019)
AMERICAN INSTITUTE OF STEEL CONSTRUCTION (AISC 15TH EDITION)
AMERICAN SOCIETY OF CIVIL ENGINEERS (ASCE 7-16)

CIVIL ENGINEERING DESIGN STANDARDS

VA SITE DEVELOPMENT DESIGN MANUAL — APRIL 1, 2021
INTERNATIONAL BUILDING CODE (IBC) — 2018

EHRM PROGRAM DESIGN ALERTS

00 VA OEHRM SITE INFRASTRUCTURE REQUIREMENTS V2.0
SOCAMES 6 DESIGN ALERT 1 - 11

PROJECT TEAM

OWNER

Chilliloth VA Medical Center

Trent Vartorella, CDR
17273 state route 104
Chilliloth, OH 45601-9715

CIVIL ENGINEER

GDM-AE, Inc.

Celyn Dezmain
1308 NE 134th Street, Suite A
Vancouver, WA 98685

MECHANICAL ENGINEER

GDM-AE, Inc.

Scotten Blair
1308 NE 134th Street, Suite A
Vancouver, WA 98685

FIRE PROTECTION

GDM-AE, Inc.

Conrad Chandler
1308 NE 134th Street, Suite A
Vancouver, WA 98685

ARCHITECT

GDM-AE, Inc.

Eric Shreve
1308 NE 134th Street, Suite A
Vancouver, WA 98685

ELECTRICAL ENGINEER

GDM-AE, Inc.

Alex Walker
1308 NE 134th Street, Suite A
Vancouver, WA 98685

PLUMBING ENGINEER

GDM-AE, Inc.

Scotten Blair
1308 NE 134th Street, Suite A
Vancouver, WA 98685

COST ESTIMATOR

PRO DIMS

Dennis Teschong
520 Kirkland Way, Suite 301
Kirkland WA, 98033-6256

ERM CONSULTANT

AMERICAN ENGINEERING TESTING

Bruce Bohman
550 Cleveland Avenue North
St. Paul, MN 55114-1804

TYPICAL ABBREVIATIONS				GENERAL NOTES				DRAWING INDEX			
AE	ARCHITECT/ENGINEER	(E)	EXISTING	IBC	INTERNATIONAL BUILDING CODE	R	RADIUS OR RISER	PG	SHEET	DRAWING TITLE	
ACT	ACOUSTICAL CEILING TILE	EA	EACH	ID	IDENTIFICATION, INSIDE DIAMETER, OR INTERIOR DESIGN	RA	RETURN AIR				
AC	AIR CONDITIONING	EB	EXPANSION BOLT	INCL	INCLUDED	RAD	RADIATOR				
ADA	AMERICANS WITH DISABILITIES ACT	EF	EXHAUST FAN	IN	INFORMATION	RB	RUBBER BASE OR RESILIENT BASE				
ADJ	ADJACENT, ADJOINING, OR ADJUSTABLE	EFS	EXTERIOR FINISH SYSTEM	INFO	INCHES	RCP	REFLECTED CEILING PLAN				
AFC	ABOVE FINISHED COUNTER	EIFS	EXTERIOR INSULATION & FINISH SYSTEM	INSUL	INSULATION	RD	ROAD OR ROOF DRAIN				
AFF	ABOVE FINISHED FLOOR					REC	RECESSED				
AFG	ABOVE FINISHED GRADE	EJ	EXPANSION JOINT	JAN	JANITOR	RECPT	RECTEAPCTANGLE				
AFS	ABOVE FINISHED SLAB	ELAST	ELASTOMERIC	JST	JOIST	RECT	RECTANGLE				
AHU	AIR HANDLING UNIT	ELEV	ELEVATION, OR ELEVATOR	JOIST	JOIST	REF	REFERENCE				
AISC	AMERICAN INSTITUTE OF STEEL	EMER	EMERGENCY	JT	JOINT	REG	REGISTER				
AIB	CONSTRUCTION	ENGR	ENGINEER	KPL	KICKPLATE	REIN	REINFORCE				
ALT	ALTERNATE	ENVR	ENVIRONMENT			REP	REPAIR				
ALUM	ALUMINUM	EPA	ENVIRONMENTAL PROTECTION AGENCY			REPL	REPLACE				
AMP	AMPERE	EPDM	ETHYLENE PROPYLENE DIENE	L	ANGLE	REQ	REQUIRE				
AMT	AMOUNT	EPS	EXPANDED POLYSTYRENE BOARD (INSULATION)	LAB	LABORATORY	REQD	REQUIRED				
ANOD	ANODIZE	EQ	EQUAL	LAM	LAMINATE	RESIL	RESILIENT				
ANSI	AMERICAN NATIONAL STANDARDS	EQL SP	EQUALLY SPACED	LAM GL	LAMINATED GLASS	RET	RETURN				
APA	AMERICAN PLYWOOD ASSOCIATION	EQ	EQUIPMENT	LAU	LAUNDRY	REV	REVISION				
APPROX	APPROXIMATE	ESMT	EASEMENT	LAV	LAVATORY	RFI	REQUEST FOR INFORMATION				
ARCH	ARCHITECT	EST	ESTIMATE	LBR	LUMBER	RFP	REQUEST FOR PROPOSAL				
ASI	ARCHITECT'S SUPPLEMENTAL INSTRUCTION	EXIST	EXISTING	LBS	POUND	RH	RIGHT HAND				
ASPH	ASPHALT	EXP	EXPANSION OR EXPOSED	LED	LIGHT EMITTING DIODE	RHR	RIGHT HAND REVERSE				
ASTM	AMERICAN SOCIETY FOR TESTING AND MATERIALS	EXP BT	EXPANSION BOLT	LH	LEFT HAND	RLG	RAILING				
AUTO	TESTING AND MATERIALS	EXT	EXTENDING GRADE	LHR	LEFT HAND REVERSE	RM	ROOM				
AUX	AUTOMATIC	EXT GR	EXTERIOR, EXTERNAL, OR EXTINGUISHER	LIB	LIBRARY	RO	ROUGH OPENING				
AVE	AVENUE			LIN	LINEAR	ROW	RIGHT OF WAY				
AVG	AVERAGE	F	FAHRENHEIT OR FEMALE	LINO	LINOLEUM	RS	REVOLUTIONS PER MINUTE				
AWI	ARCHITECTURAL WOODWORKING INSTITUTE	FA	FIRE ALARM	LQ	LIQUID	RSG	ROUGH SAWN				
AWPA	AMERICAN WOOD PRESERVERS ASSOCIATION	FDC	FIRE DEPARTMENT CONNECTION	LNDSCP	LANDSCAPE	S	SOUTH				
		FDTN	FOUNDATION	LR	LIVING ROOM	SA	SUPPLY AIR				
		FE	FIRE EXTINGUISHER	LRS	LARGE	SBS	STYRENE BUTADIEN STYRENE				
		FEC	FIRE EXTINGUISHER & CABINET	LS	LUMP SUM	SBSST	SUBSTRATE				
		FF	FINISH FACE	LT GA	LIGHT GAGE	SHED	SHED				
		FF EL	FINISH FLOOR ELEVATION	LT WT	LIGHTWEIGHT	S	SOUTH				
		FFEL	FURNITURE, FIXTURE, AND EQUIPMENT	LVR	LOUVER	SAV	SALVAGE				
		FG	FINISH GRADE			SECT	SECTION				
		FHC	FIRE HOSE CABINET			SEP	SEPARATION				
		FIG	FIGURE			SQ	SQUARE				
		FIN	FINISH			SQ YD	SQ YD				
		FIN FLR	FINISH FLOOR			ST	STEEL				
		FIN GR	FINISH GRADE			STL	STEEL				
		FIN WD	FINISH WOOD			STC	STEEL				
		FL	FLOORLINE			STC	STEEL				
		FLASH	FLASHING			STC	STEEL				
		FLEX	FLEXIBLE			STC	STEEL				
		FLR	FLOOR			STC	STEEL				
		FLR FIN	FLOOR FINISH			STC	STEEL				
		FLR SK	FLOOR SINK			STC	STEEL				
		FLUOR	FLUORESCENT			STC	STEEL				
		FLUOR FIX	FLUORESCENT FIXTURE			STC	STEEL				
		FM	FACTORY MUTUAL			STC	STEEL				
		FO	FINISHED OPENING			STC	STEEL				
		FOC	FACE OF CONCRETE OR FACE OF CURB			STC	STEEL				
		FOF	FACE OF FINISH			STC	STEEL				
		FOM	FACE OF MASONRY			STC	STEEL				
		FOS	FACE OF STUD			STC	STEEL				
		FOW	FACE OF WALL			STC	STEEL				
		FR	FIRE RATING, FIRE RESISTANT, OR FRAME			STC	STEEL				
		FRP	FIBER REINFORCED POLYESTER OR FIBER REINFORCED PLASTIC			STC	STEEL				
		FRT	FIRE RETARDANT TREATMENT			STC	STEEL				
		FRZ	FREEZER			STC	STEEL				
		FSNTR	FASTENER			STC	STEEL				
		FT	FOOT OR FEET			STC	STEEL				
		FTG	FOOTING			STC	STEEL				
		FURG	FURRING			STC	STEEL				
		FURN	FURNISH OR FURNITURE			STC	STEEL				
						STC	STEEL				
						STC	STEEL				
F

IX.

IX.



NEW FINISHED GRADE (EXISTING ELEVATION) POINT ID	679.45 (679.46)
NEW FINISHED GRADE MEET EXISTING ELEVATION POINT ID	679.45 MEG

00-CS-001

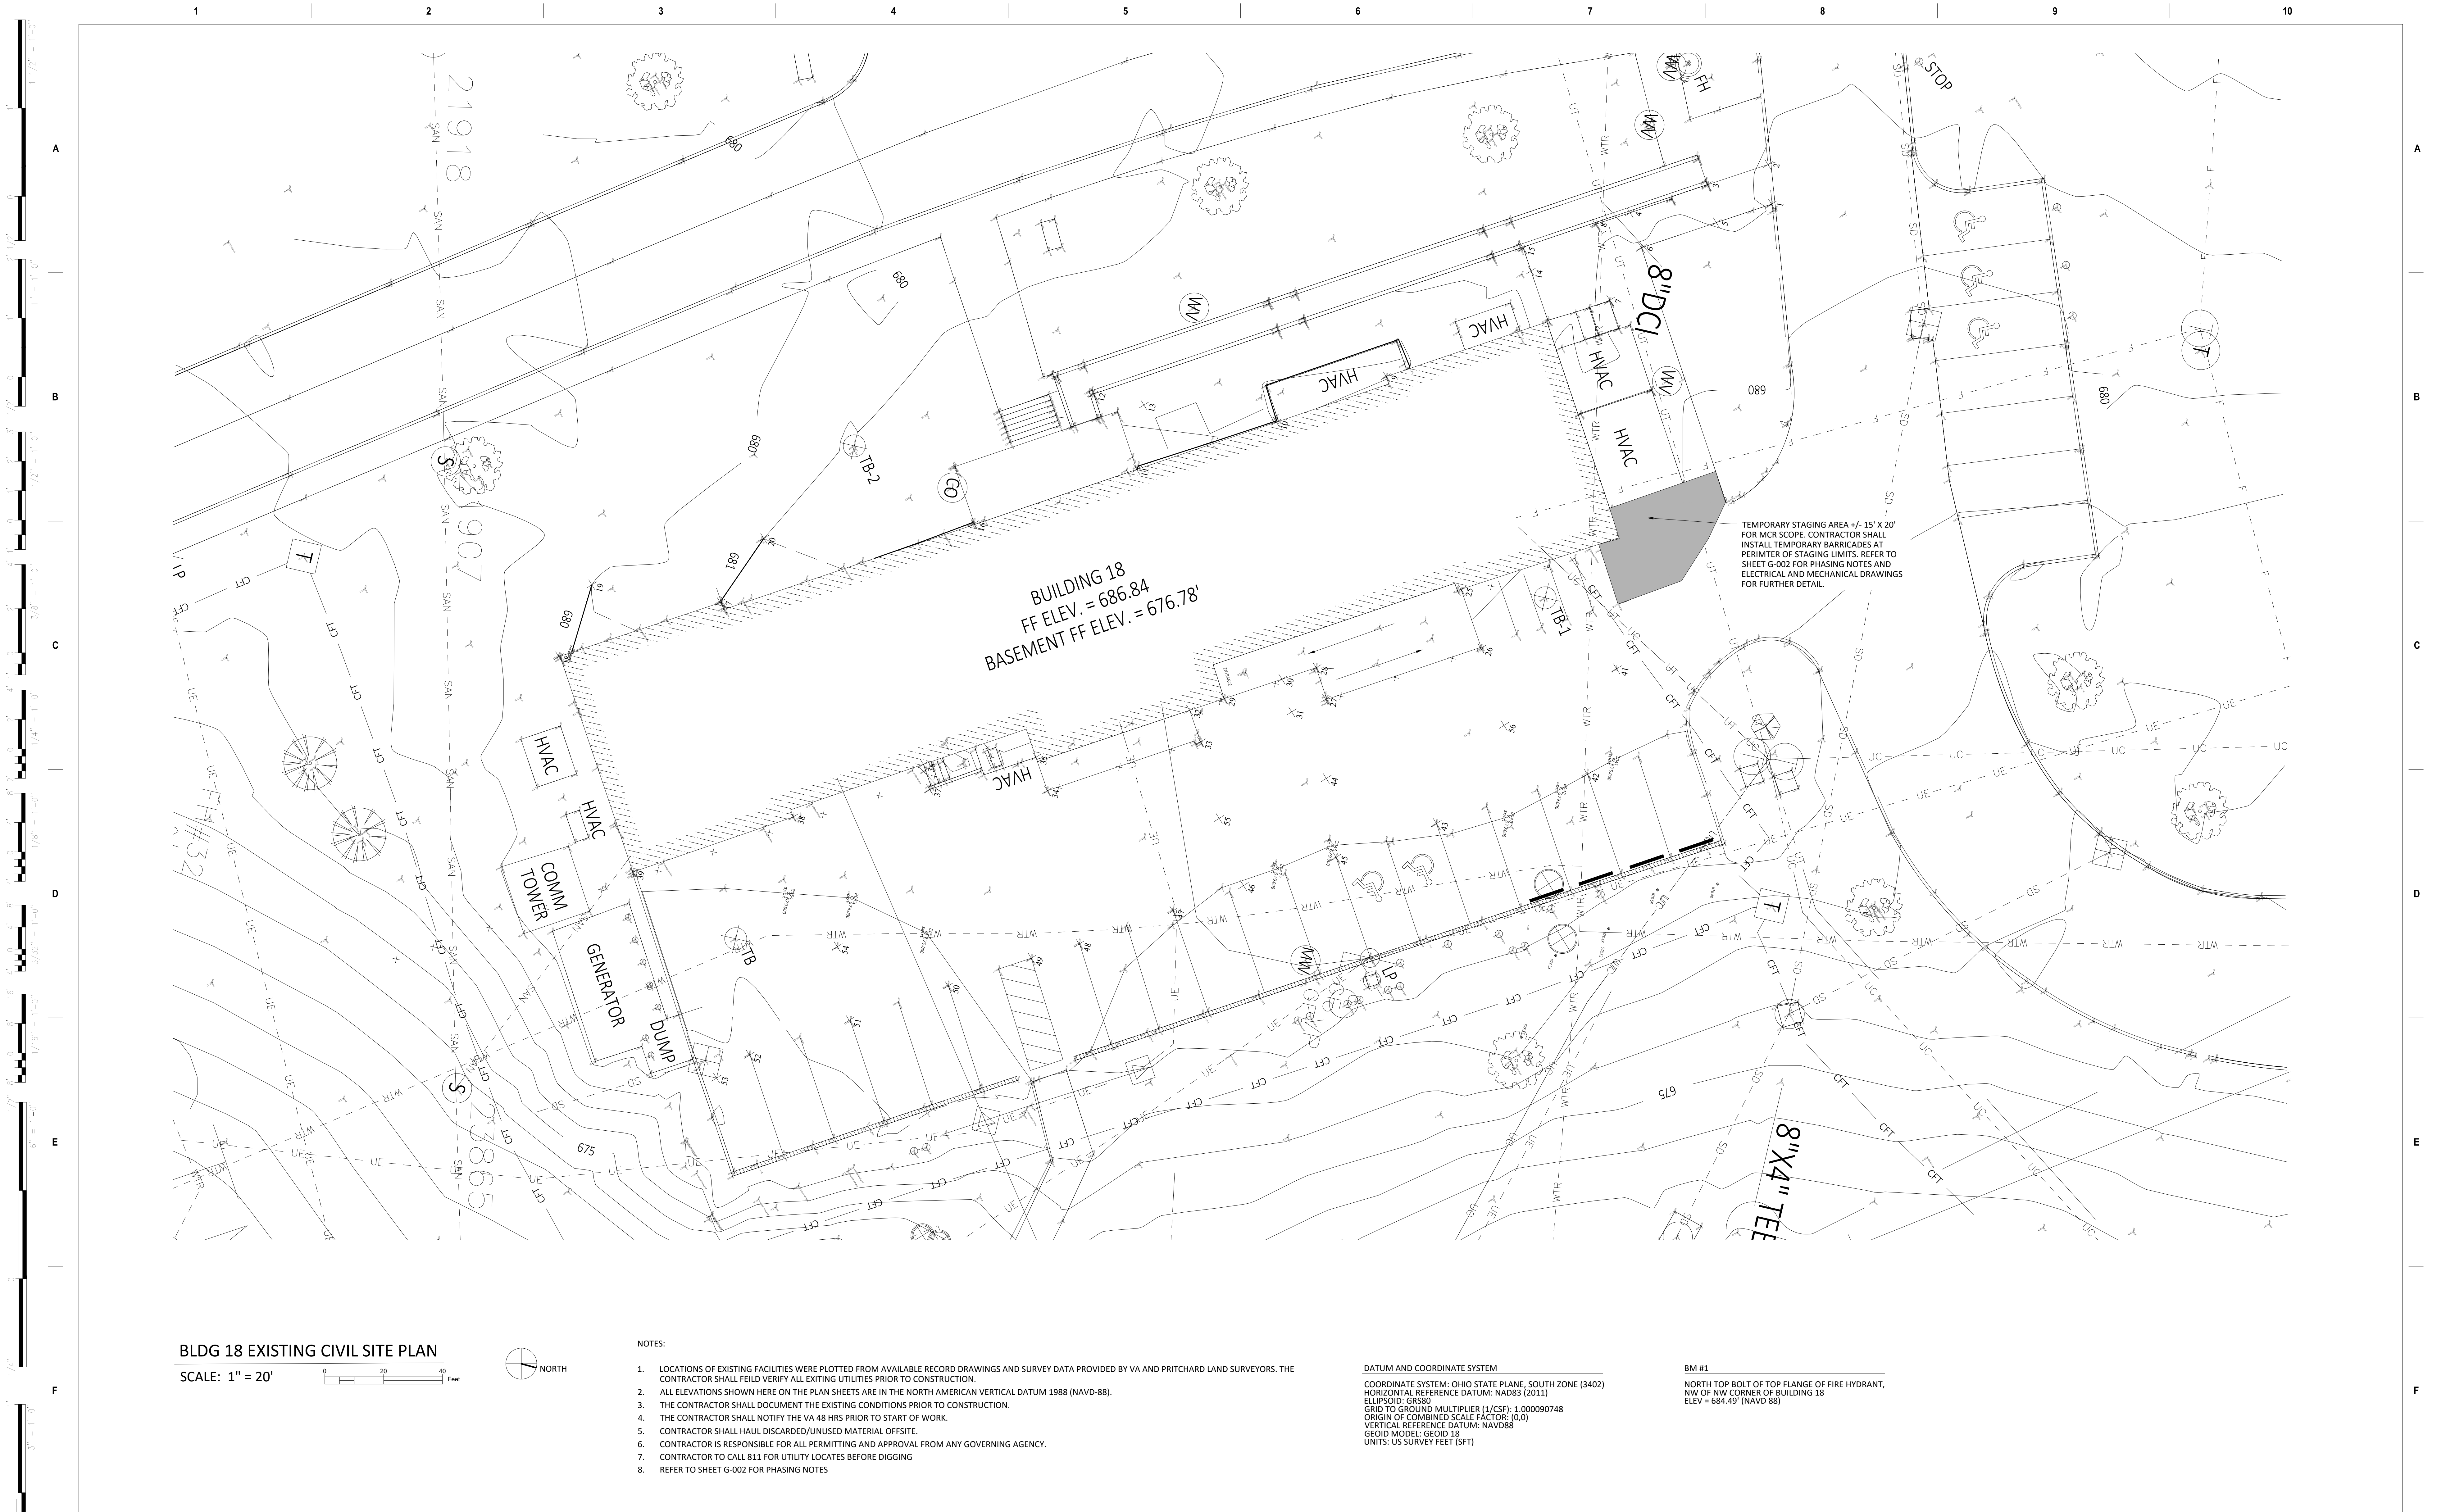

BLDG 18 EXISTING CIVIL SITE PLAN

SCALE: 1" = 20'

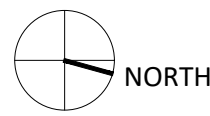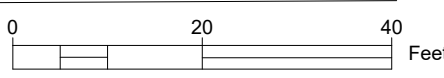

NOTES:

1. LOCATIONS OF EXISTING FACILITIES WERE PLOTTED FROM AVAILABLE RECORD DRAWINGS AND SURVEY DATA PROVIDED BY VA AND PRITCHARD LAND SURVEYORS. THE CONTRACTOR SHALL FIELD VERIFY ALL EXISTING UTILITIES PRIOR TO CONSTRUCTION.
2. ALL ELEVATIONS SHOWN HERE ON THE PLAN SHEETS ARE IN THE NORTH AMERICAN VERTICAL DATUM 1988 (NAVD-88).
3. THE CONTRACTOR SHALL DOCUMENT THE EXISTING CONDITIONS PRIOR TO CONSTRUCTION.
4. THE CONTRACTOR SHALL NOTIFY THE VA 48 HRS PRIOR TO START OF WORK.
5. CONTRACTOR SHALL HAUL DISCARDED/UNUSED MATERIAL OFFSITE.
6. CONTRACTOR IS RESPONSIBLE FOR ALL PERMITTING AND APPROVAL FROM ANY GOVERNING AGENCY.
7. CONTRACTOR TO CALL 811 FOR UTILITY LOCATES BEFORE DIGGING
8. REFER TO SHEET G-002 FOR PHASING NOTES


DATUM AND COORDINATE SYSTEM

COORDINATE SYSTEM: OHIO STATE PLANE, SOUTH ZONE (3402)
HORIZONTAL REFERENCE DATUM: NAD83 (2011)
ELLIPSOID: GR80
GRID TO GROUND MULTIPLIER (1/CSF): 1.000090748
ORIGIN OF COMBINED SCALE FACTOR: (0,0)
VERTICAL REFERENCE DATUM: NAVD83
GEOID MODEL: GEOID 18
UNITS: US SURVEY FEET (SFT)

BM #1



NORTH TOP BOLT OF TOP FLANGE OF FIRE HYDRANT,
NW OF NW CORNER OF BUILDING 18
ELEV = 684.49' (NAVD 88)

Revisions: 10% BASIS OF DESIGN 35% SCHEMATIC DESIGN 65% DESIGN DEVELOPMENT 95% CONSTRUCTION DOCUMENTS	Date: 08-27-2023 11-08-2023 04-07-2025 06-12-2025	CONSULTANT CONSULTANT:	ARCHITECT/ENGINEER OF RECORD GDM-AE, Inc. 1308 NE 134TH ST SUITE A VANCOUVER, WA 98685 P: 541.426.4723 WILL GORDON, CEO WWW.GDM-AE.COM	STAMP GDM ARCHITECTS • ENGINEERS	PROGRAM CONTRACTING ACTIVITY CENTRAL (PCAC) VA U.S. Department of Veterans Affairs	DRAWING TITLE BUILDING 18 - EXISTING CIVIL SITE PLAN APPROVED: FOR OFFICIAL USE ONLY (FOUO)	PHASE 100% CONSTRUCTION DOCUMENTS FLS FULLY SPRINKLERED	PROJECT TITLE VA CHILLICOTHE (EHRM) ELECTRONIC HEALTH RECORD MODERNIZATION INFRASTRUCTURE UPGRADES LOCATION 17273 STATE ROUTE 104 CHILLICOTHE, OH 45601-9718 ISSUE DATE 07/17/2025	PROJECT NO. 538-21-705 BUILDING NO. 18 DRAWING NO. 00-CS-002

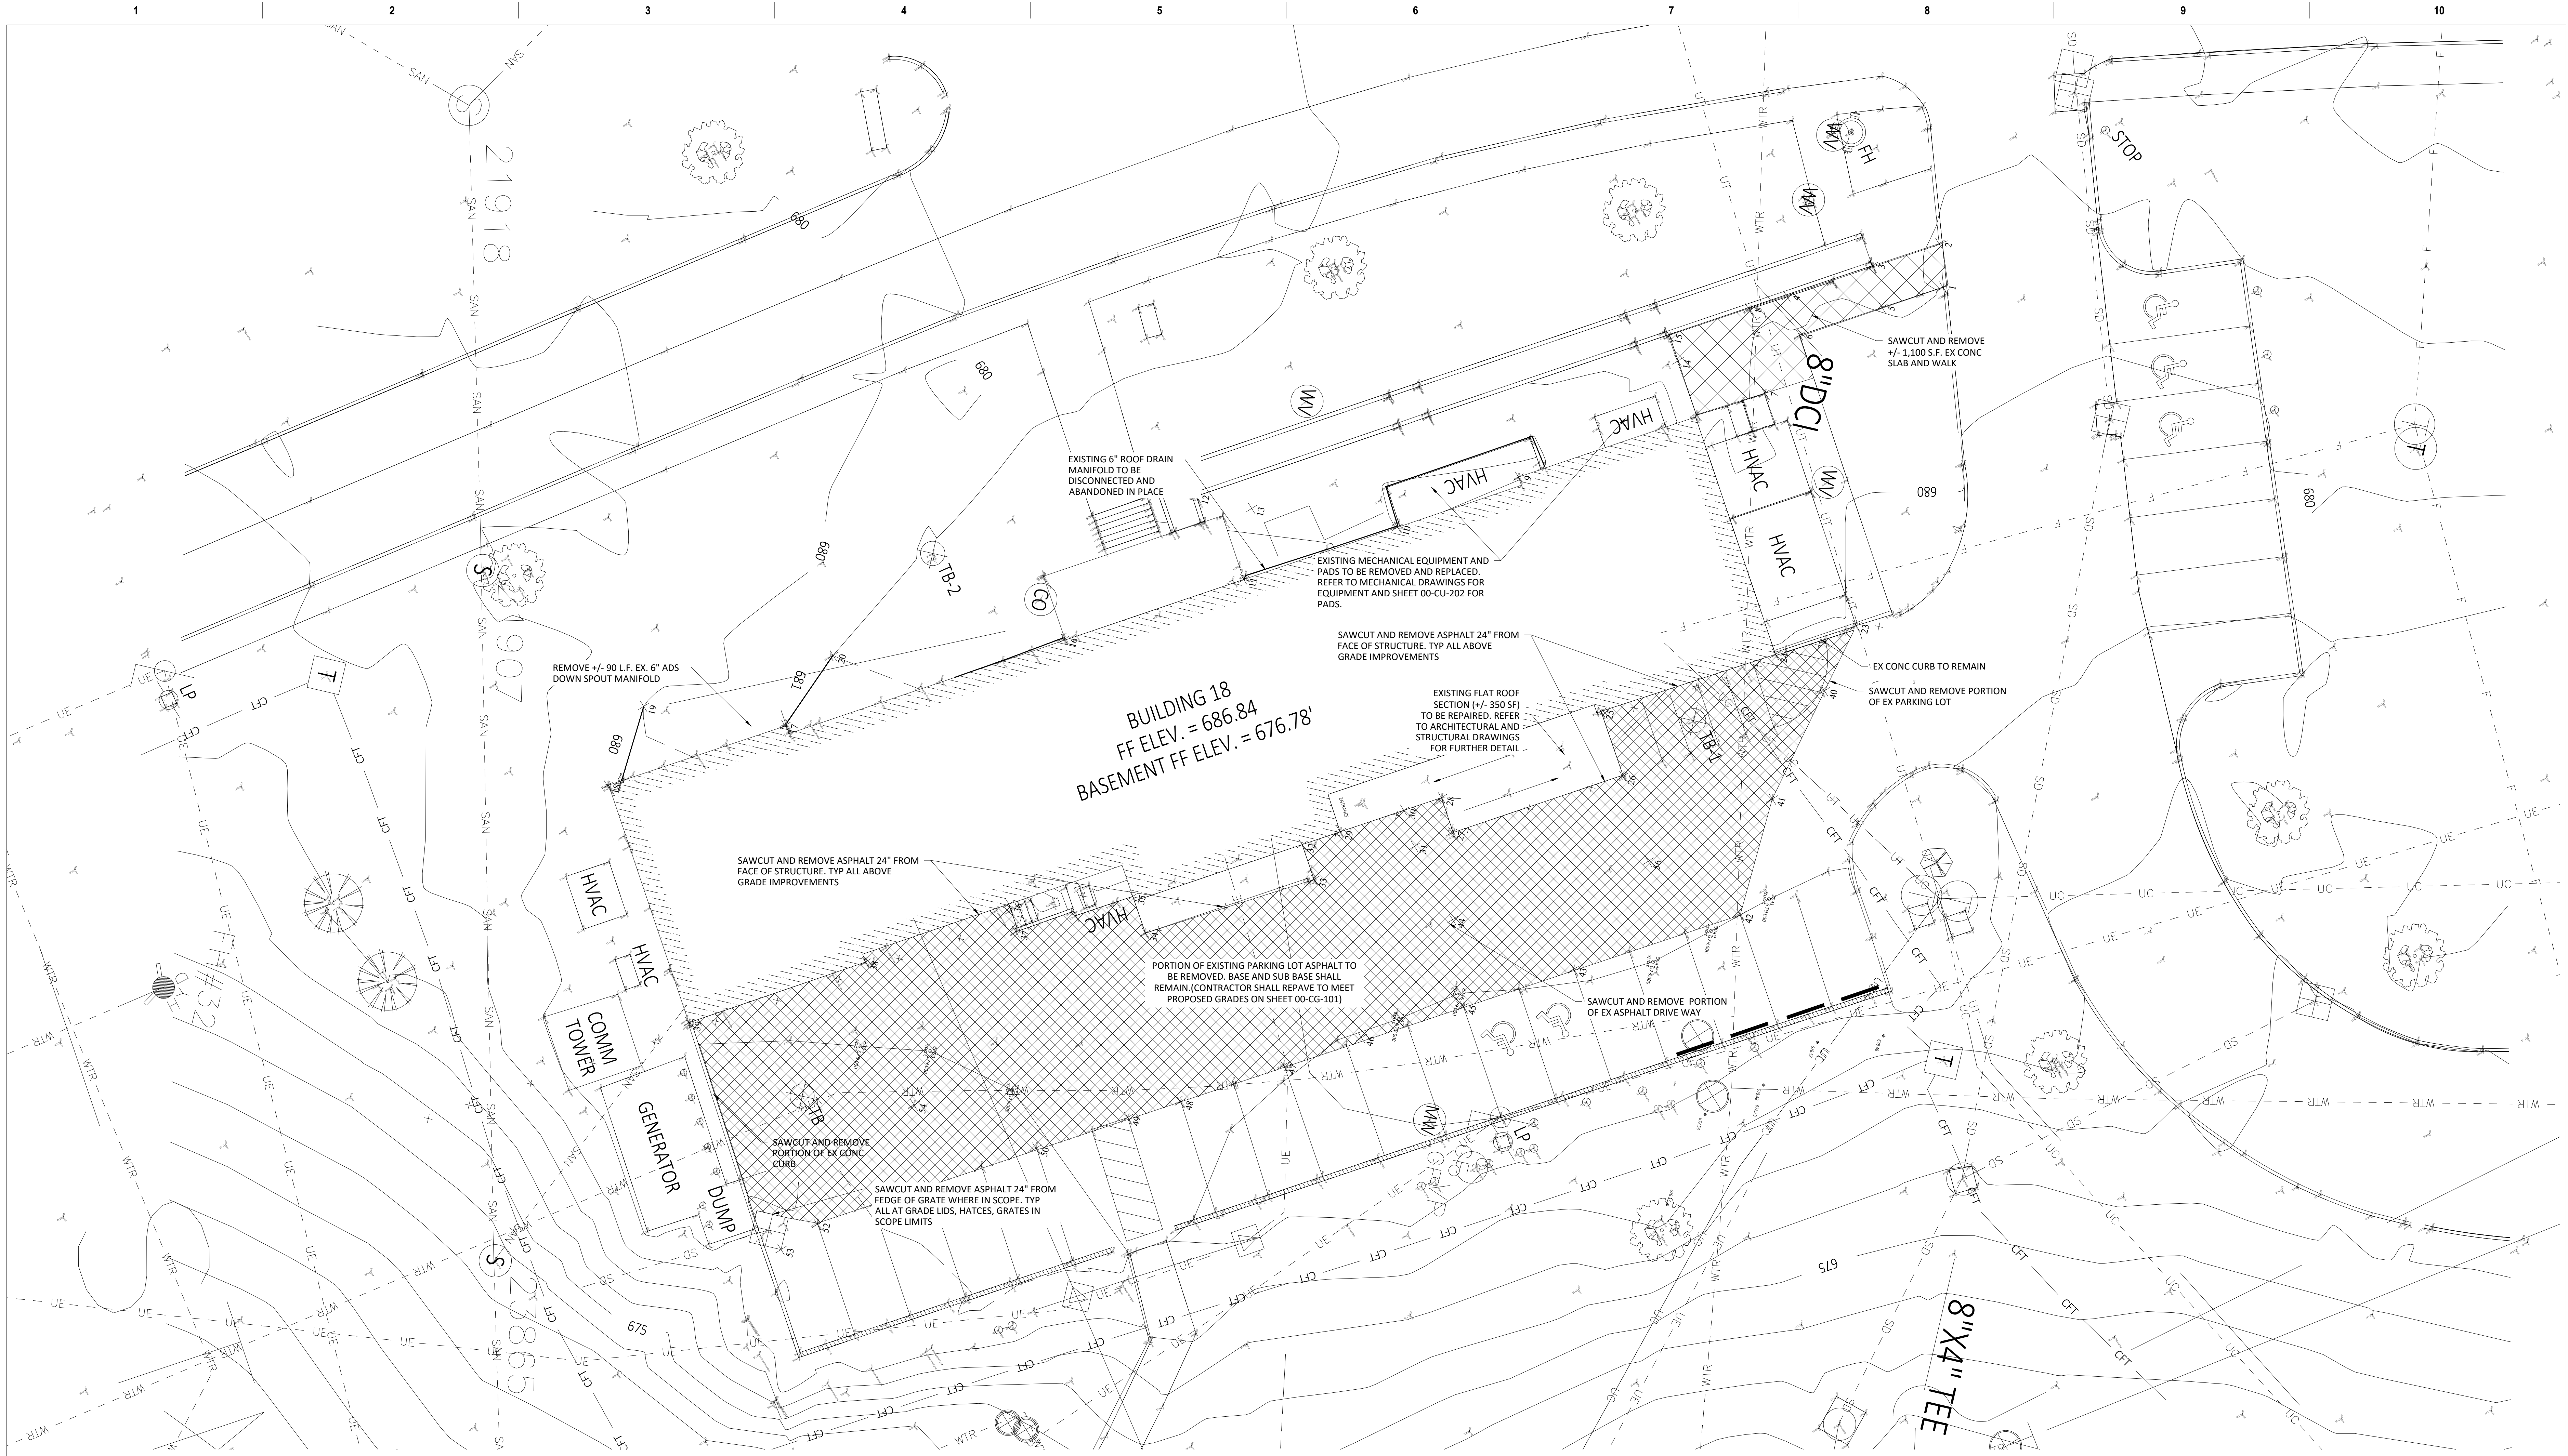

BLDG 18 CIVIL DEMOLITION PLAN

SCALE: 1" = 10'

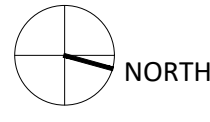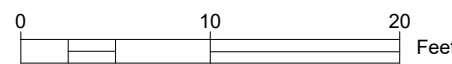

NOTES:

1. LOCATIONS OF EXISTING FACILITIES WERE PLOTTED FROM AVAILABLE RECORD DRAWINGS AND SURVEY DATA PROVIDED BY VA. THE CONTRACTOR SHALL FIELD VERIFY ALL EXISTING UTILITIES PRIOR TO CONSTRUCTION.
2. ALL ELEVATIONS SHOWN HERE ON THE PLAN SHEETS ARE IN THE NORTH AMERICAN VERTICAL DATUM 1988 (NAVD-88).
3. THE CONTRACTOR SHALL DOCUMENT THE EXISTING CONDITIONS PRIOR TO CONSTRUCTION.
4. THE CONTRACTOR SHALL NOTIFY THE VA 48 HRS PRIOR TO START OF WORK.
5. CONTRACTOR SHALL HAUL DISCARDED/UNUSED MATERIAL OFFSITE.
6. CONTRACTOR IS RESPONSIBLE FOR ALL PERMITTING AND APPROVAL FROM ANY GOVERNING AGENCY.
7. CONTRACTOR TO CALL 811 FOR UTILITY LOCATES BEFORE DIGGING
8. REFER TO SHEET G-002 FOR PHASING NOTES.

Revisions:	10% BASIS OF DESIGN	Date:	08-27-2023
	35% SCHEMATIC DESIGN		11-08-2023
	65% DESIGN DEVELOPMENT		04-07-2025
	95% CONSTRUCTION DOCUMENTS		06-12-2025

CONSULTANT


CONSULTANT:

ARCHITECT/ENGINEER OF RECORD

GDM-AE, Inc.
1308 NE 134TH ST SUITE A
VANCOUVER, WA 98685
P: 541.426.4723
WILL GORDON, CEO
WWW.GDM-AE.COM

GDM
ARCHITECTS • ENGINEERS

STAMP

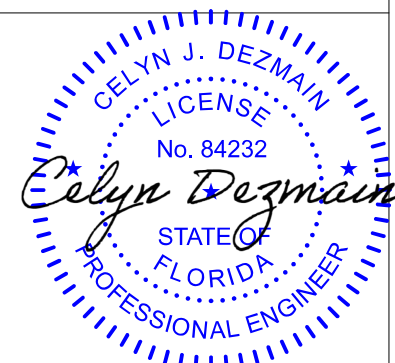

PROGRAM
CONTRACTING
ACTIVITY
CENTRAL (PCAC)



U.S. Department
of Veterans Affairs

DRAWING TITLE

BUILDING 18 - CIVIL DEMOLITION
PLAN

APPROVED:

FOR OFFICIAL USE ONLY (FOUO)

PHASE

100% CONSTRUCTION
DOCUMENTS

FLS

FULLY
SPRINKLERED

PROJECT TITLE

VA CHILLICOTHE (EHRM) ELECTRONIC
HEALTH RECORD MODERNIZATION
INFRASTRUCTURE UPGRADES

LOCATION

17273 STATE ROUTE 104
CHILLICOTHE, OH 45601-9718

ISSUE DATE
07/17/2025

CHECKED BY
CD

DRAWN BY
DT

PROJECT NO.


538-21-705

BUILDING NO.

18



DRAWING NO.

00-CD-101

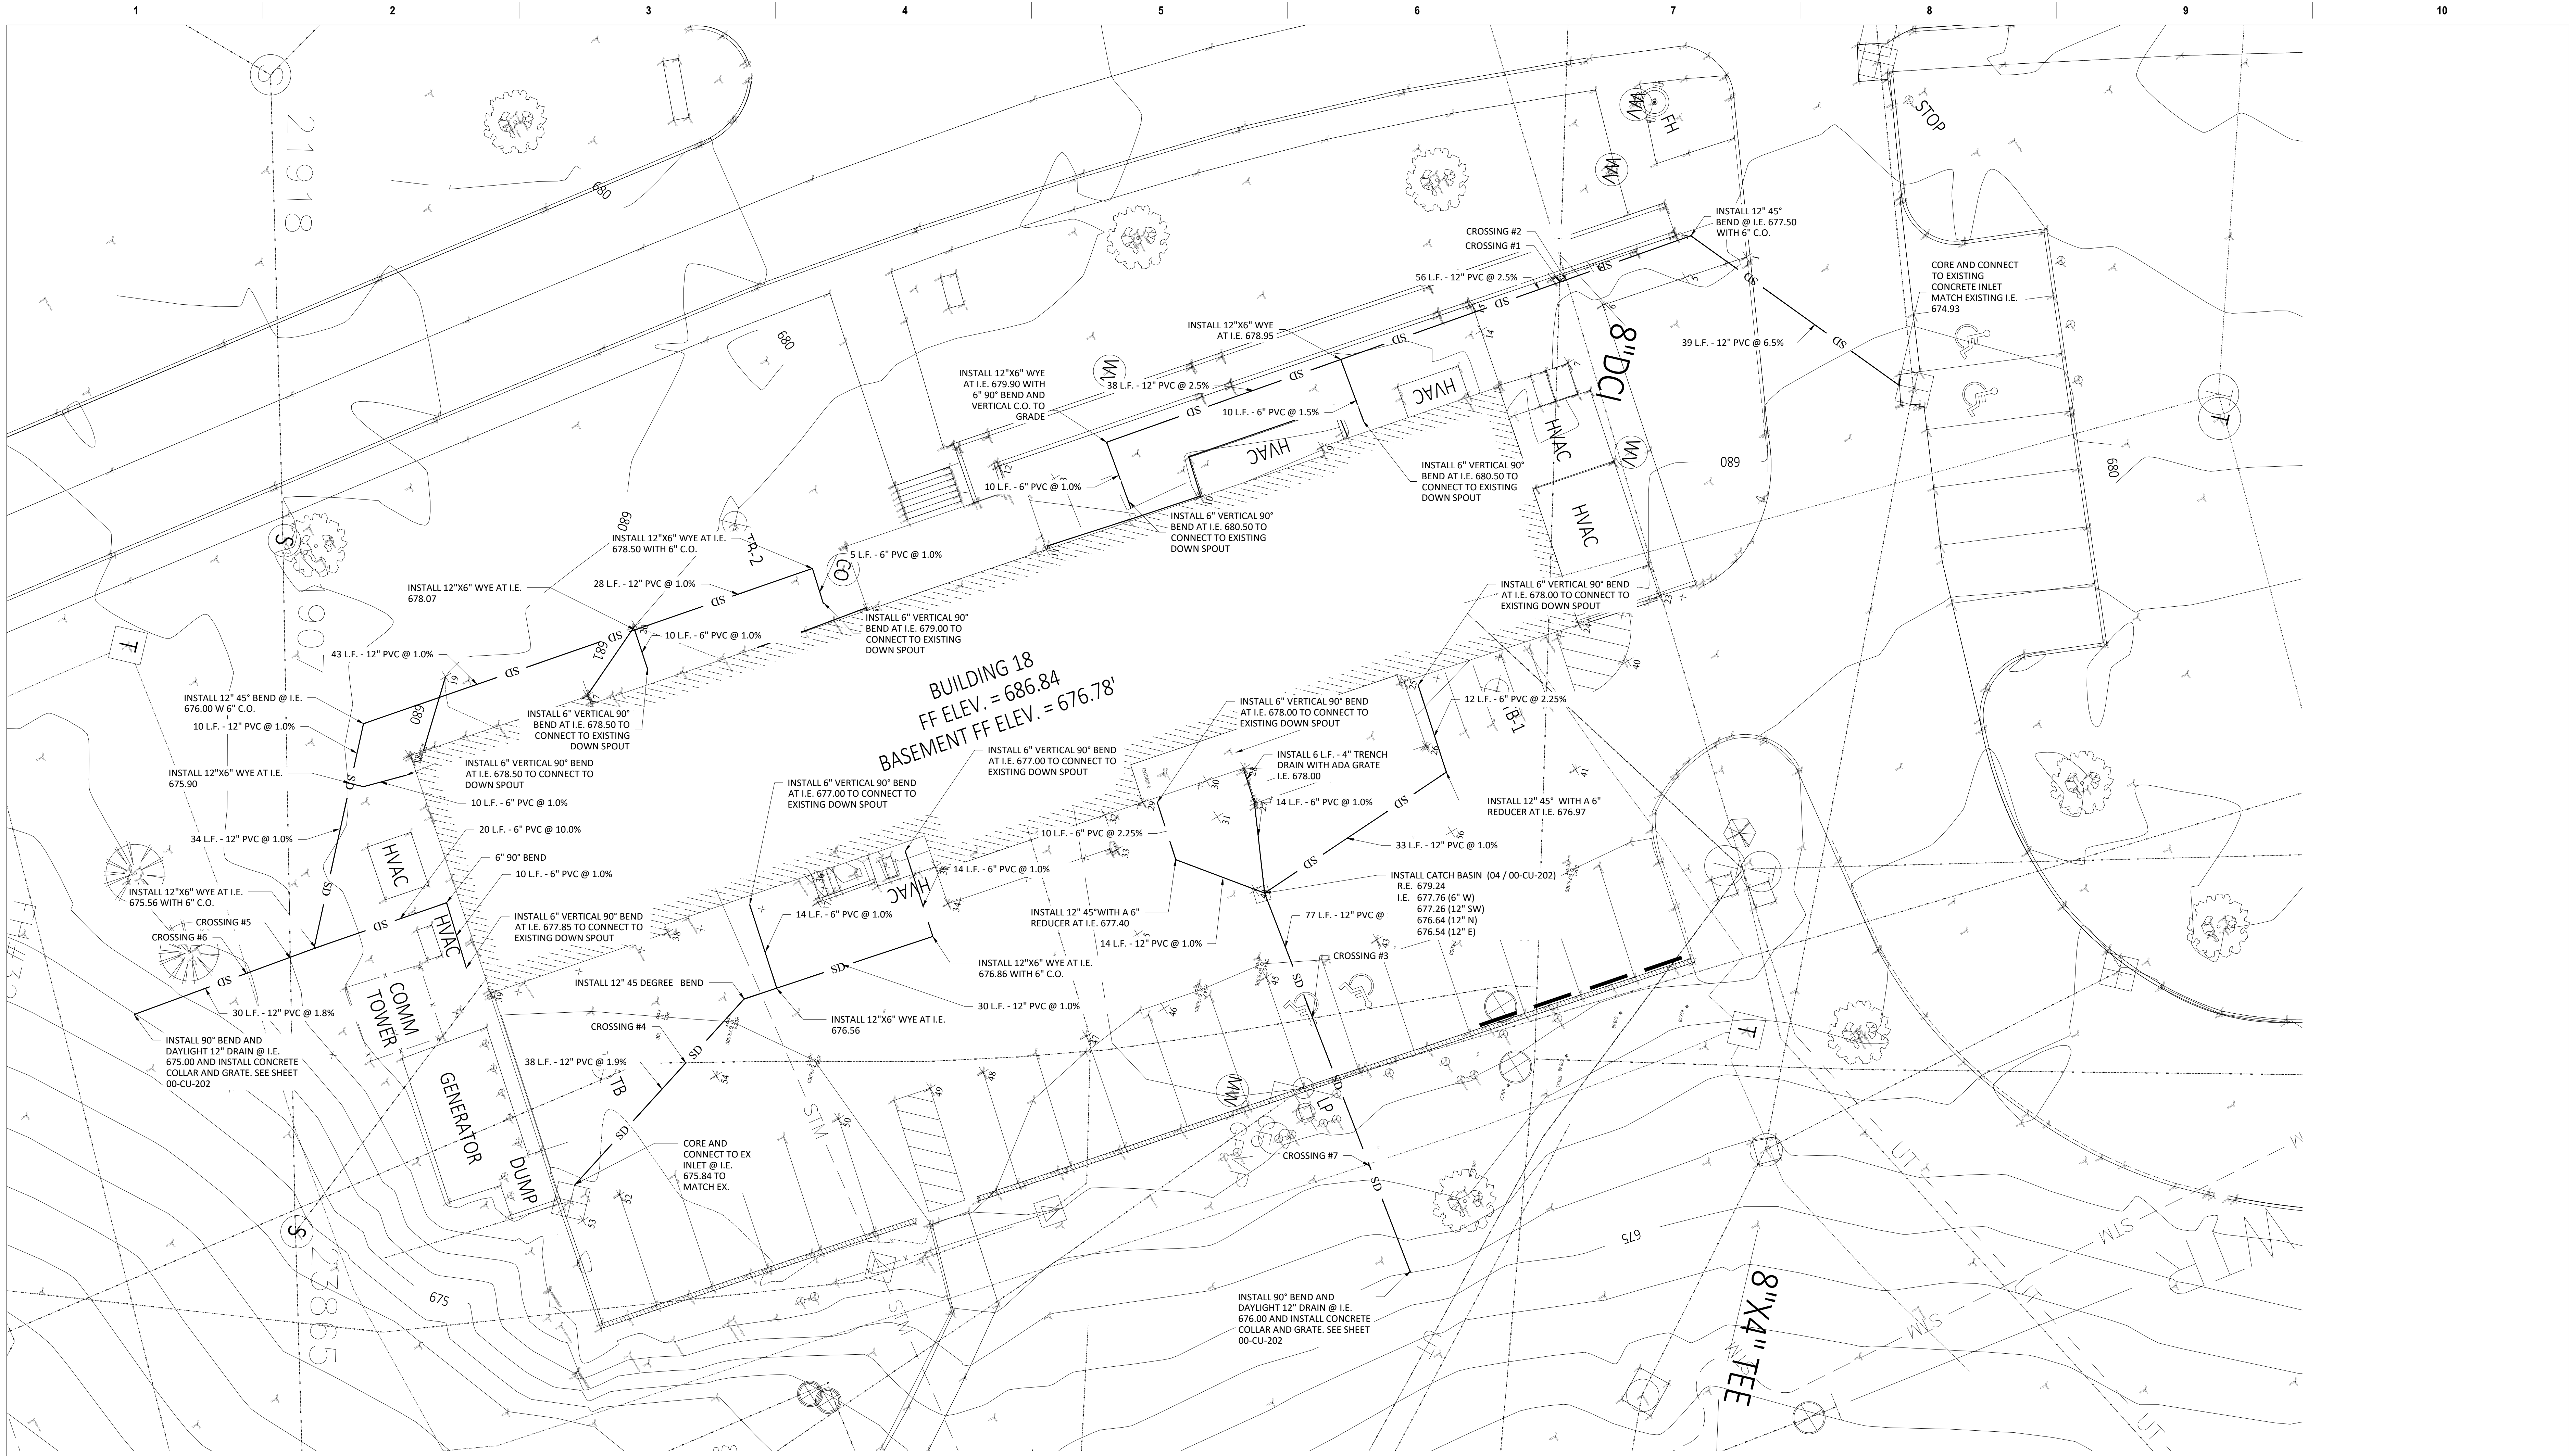

BLDG 18 CIVIL DRAINAGE PLAN

SCALE: 1" = 10'

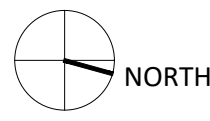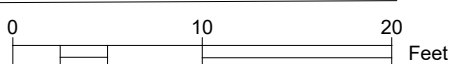

NOTES:

- LOCATIONS OF EXISTING FACILITIES WERE PLOTTED FROM AVAILABLE VA RECORD DRAWINGS AND SURVEY DATA PROVIDED BY PRITCHARD LAND SURVEYORS. THE CONTRACTOR SHALL FIELD VERIFY ALL EXISTING UTILITIES PRIOR TO CONSTRUCTION.
- ALL ELEVATIONS SHOWN HERE ON THE PLAN SHEETS ARE IN THE NORTH AMERICAN VERTICAL DATUM 1988 (NAVD-88).
- THE CONTRACTOR SHALL DOCUMENT THE EXISTING CONDITIONS PRIOR TO CONSTRUCTION.
- THE CONTRACTOR SHALL NOTIFY THE VA 48 HRS PRIOR TO START OF WORK.
- CONTRACTOR SHALL HAUL DISCARDED/UNUSED MATERIAL OFFSITE.
- CONTRACTOR IS RESPONSIBLE FOR ALL PERMITTING AND APPROVAL FROM ANY GOVERNING AGENCY.
- CONTRACTOR TO CALL 811 FOR UTILITY LOCATES BEFORE DIGGING.
- ALL TRENCHING WITHIN PAVED OR HARDSCAPED AREAS SHALL RECEIVE CLEAN SAWCUTS.
- CONTRACTOR IS RESPONSIBLE FOR TEMPORARY SHORING AND FALSE WORK.

- CONTRACTOR SHALL REPAIR AND ALL DAMAGE CAUSED BY CONSTRUCTION BACK TO EXISTING OR BETTER CONDITION, INCLUDING BUT NOT LIMITED TO IRRIGATION, LANDSCAPE, HARDSCAPE, PAVEMENT, CURBING, ABOVE GRADE EQUIPMENT AND EQUIPMENT PADS, EXISTING UTILITIES (BOTH SHOWN AND NOT SHOWN ON DRAWINGS).
- CONTRACTOR MAINTAIN VERTICAL AND HORIZONTAL SEPARATION AT ALL CROSSING PER THE VA STANDARD SPECIFICATIONS.
- CONTRACTOR IS RESPONSIBLE FOR ANY AND ALL FALSEWORK, STABILIZATION, SHORING, ETC. DURING EXCAVATION AND TRENCHING TO ENSURE ALL EXISTING IMPROVEMENTS AND FACILITIES ARE SECURE AND STABILIZED.
- REFER TO SHEET G-002 FOR PHASING NOTES.

UTILITY CROSSING INDEX					
CROSSING ID	DESCRIPTION	F.G.	T.O.P BOTTOM PIPE	B.O.P TOP PIPE	SEPERATION
1	DRAIN OVER WATER	681.11	676.11	678.02	1.91
2	DRAIN OVER TELE	681.11	677	678.02	1.02
3	DRAIN OVER WATER	679.4	674.4	676.54	2.14
4	DRAIN OVER WATER	679.1	674.1	676.21	2.11
5	DRAIN OVER SANITARY	678	667.25	675.47	8.22
6	DRAIN OVER TELE	677	674	675.26	1.29
7	DRAIN OVER FIBER	678.5	675.5	676.24	0.74

Revisions:	10% BASIS OF DESIGN	Date: 08-27-2023
	35% SCHEMATIC DESIGN	11-08-2023
	65% DESIGN DEVELOPMENT	04-07-2025
	95% CONSTRUCTION DOCUMENTS	06-12-2025

CONSULTANT


CONSULTANT:

ARCHITECT/ENGINEER OF RECORD

GDM-AE, Inc.
1308 NE 134TH ST SUITE A
VANCOUVER, WA 98685
P. 541.426.4723
WILL GORDON, CEO
WWW.GDM-AE.COM



STAMP

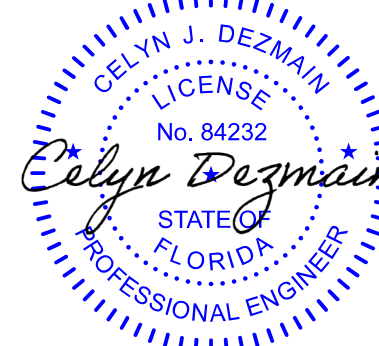

PROGRAM
CONTRACTING
ACTIVITY
CENTRAL (PCAC)



U.S. Department
of Veterans Affairs

DRAWING TITLE

BUILDING 18 - CIVIL DRAINAGE PLAN

APPROVED:

FOR OFFICIAL USE ONLY (FOUO)

PHASE

100% CONSTRUCTION
DOCUMENTS

FLS

FULLY
SPRINKLERED

PROJECT TITLE

VA CHILLICOTHE (EHRM) ELECTRONIC
HEALTH RECORD MODERNIZATION
INFRASTRUCTURE UPGRADES

LOCATION

17273 STATE ROUTE 104
CHILLICOTHE, OH 45601-9718

ISSUE DATE
07/17/2025

CHECKED BY
CD

DRAWN BY
DT

PROJECT NO.


538-21-705

BUILDING NO.

18



DRAWING NO.

00-CU-101

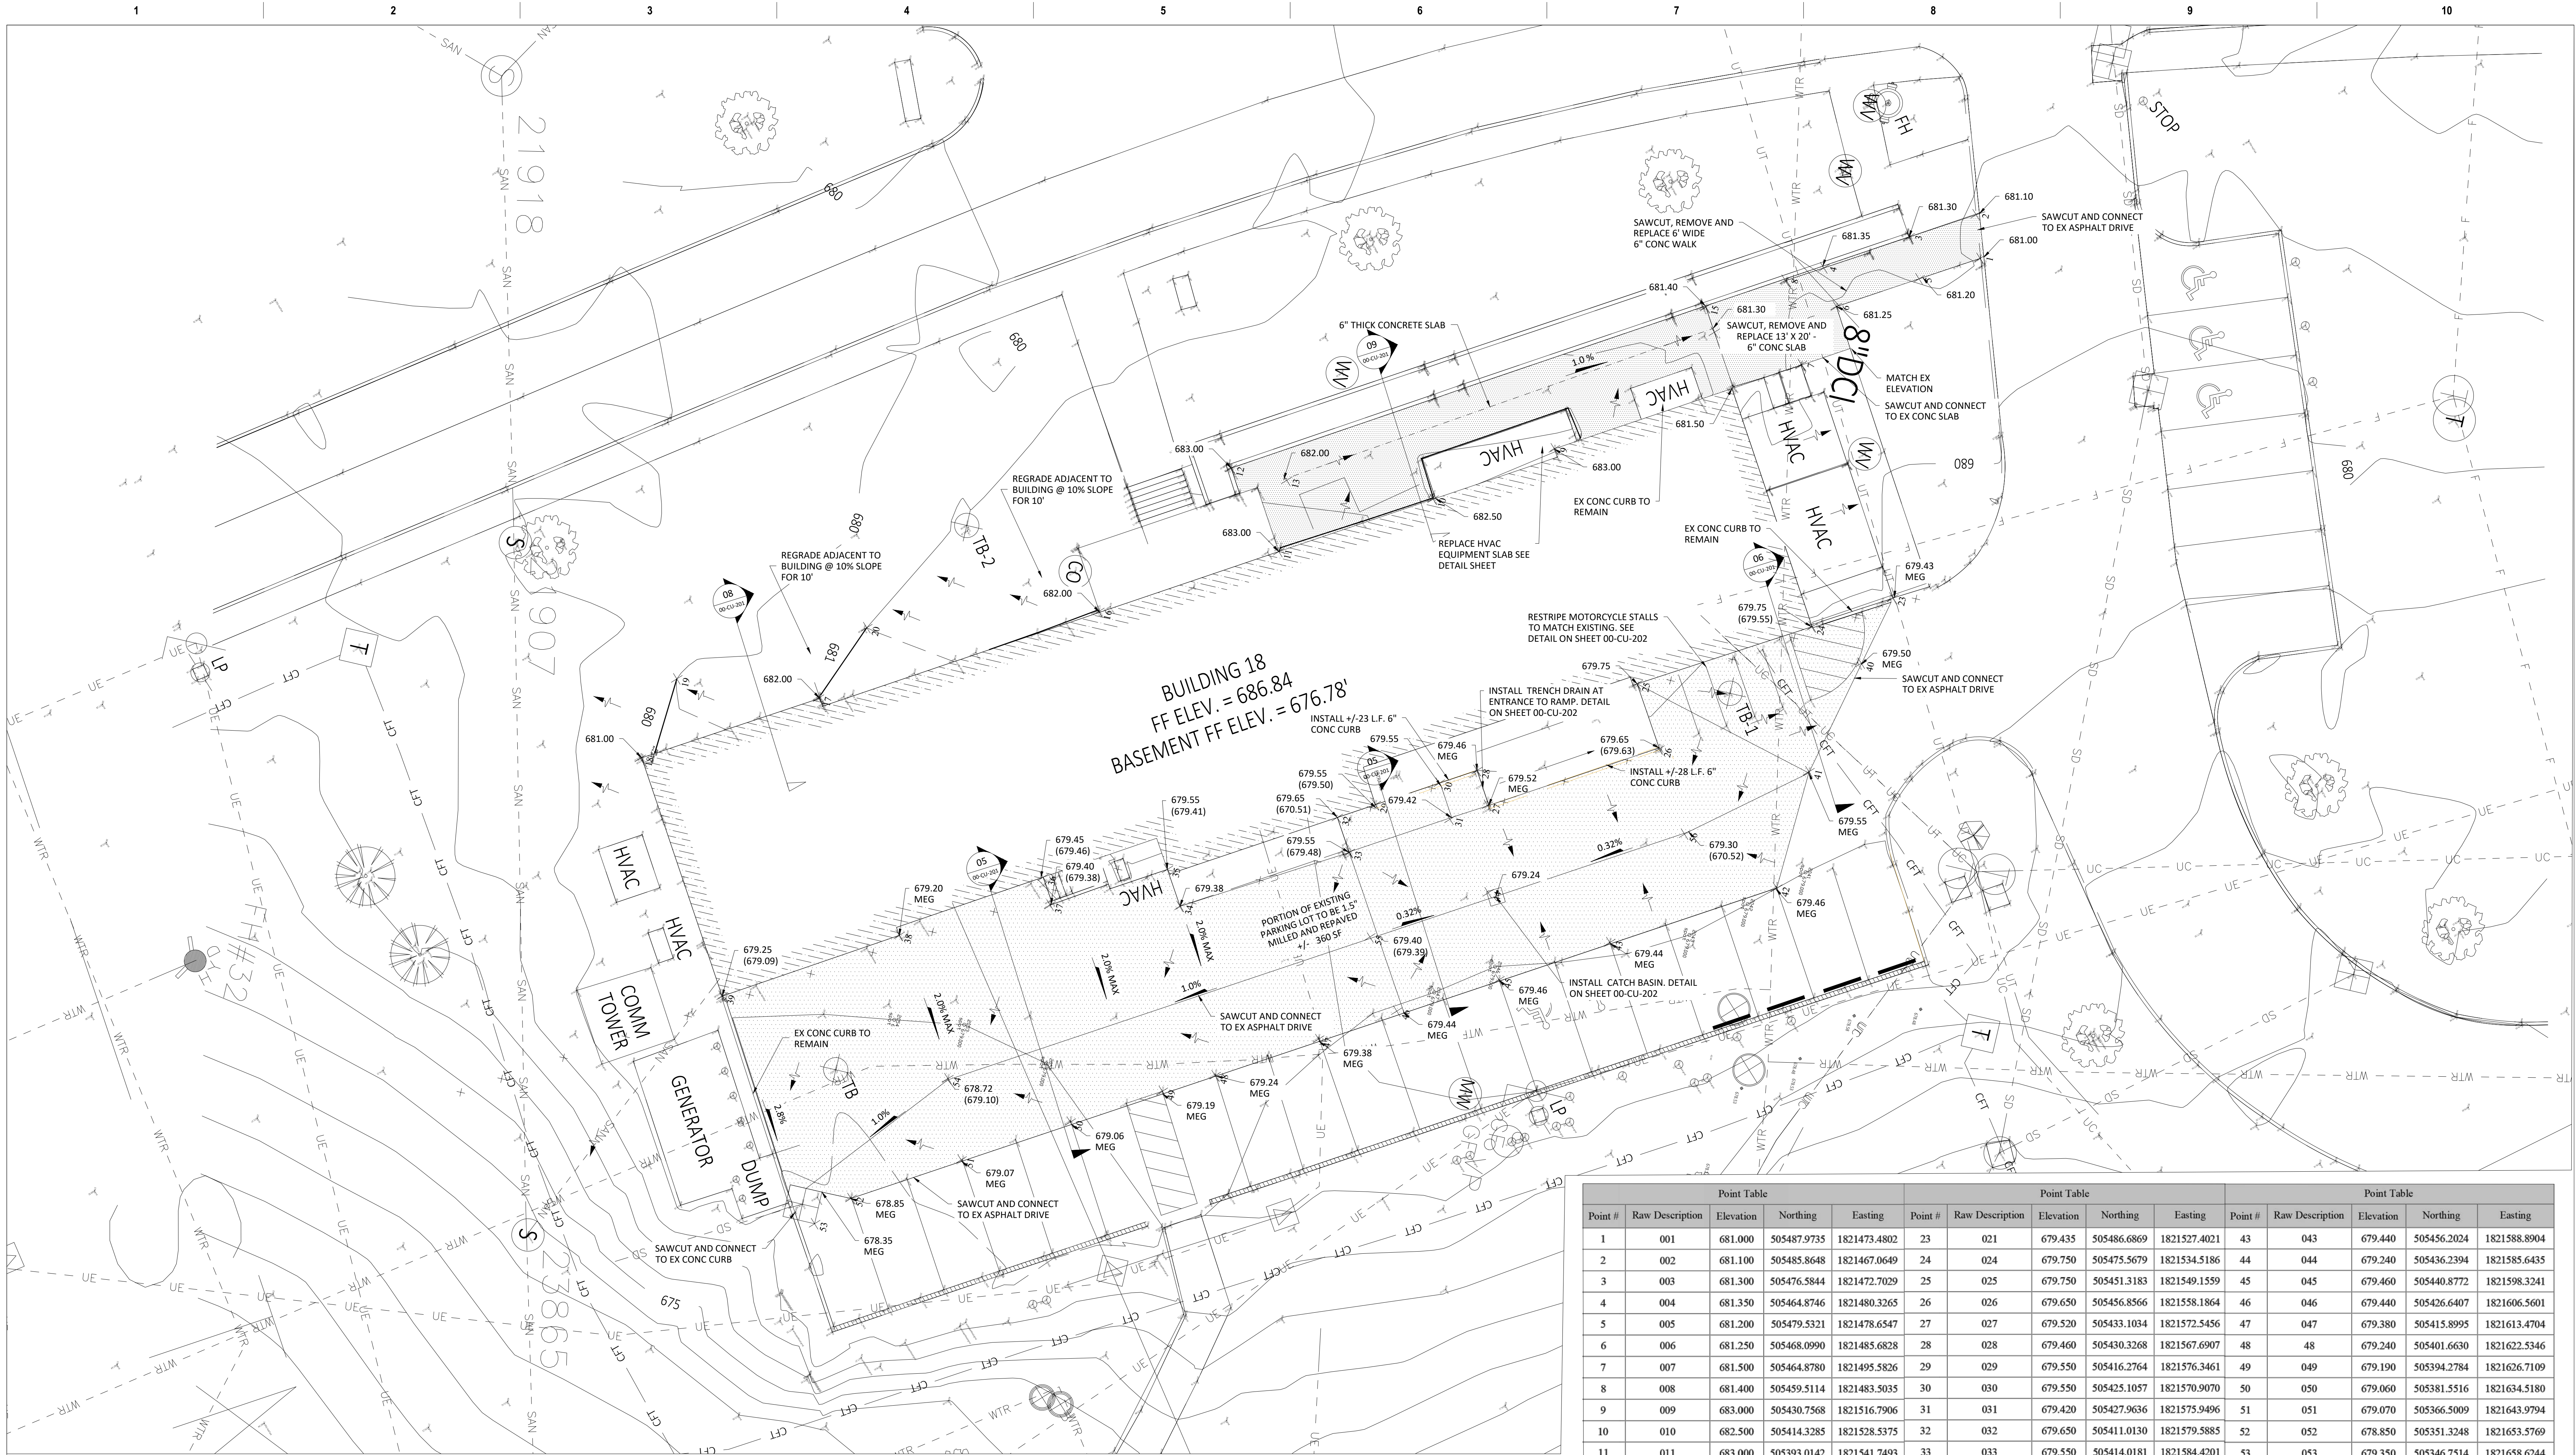

BLDG 18 CIVIL GRADING PLAN

SCALE: 1" = 10'

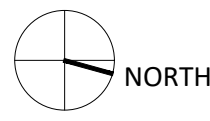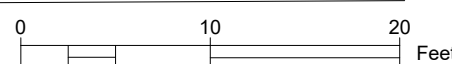

NOTES:

- LOCATIONS OF EXISTING FACILITIES WERE PLOTTED FROM AVAILABLE VA RECORD DRAWINGS AND SURVEY DATA PROVIDED BY PRITCHARD LAND SURVEYORS. THE CONTRACTOR SHALL FIELD VERIFY ALL EXISTING UTILITIES PRIOR TO CONSTRUCTION.
- ALL ELEVATIONS SHOWN HERE ON THE PLAN SHEETS ARE IN THE NORTH AMERICAN VERTICAL DATUM 1988 (NAVD-88).
- THE CONTRACTOR SHALL DOCUMENT THE EXISTING CONDITIONS PRIOR TO CONSTRUCTION.
- THE CONTRACTOR SHALL NOTIFY THE VA 48 HRS PRIOR TO START OF WORK.
- CONTRACTOR SHALL HAUL DISCARDED/UNUSED MATERIAL OFFSITE.
- CONTRACTOR IS RESPONSIBLE FOR ALL PERMITTING AND APPROVAL FROM ANY GOVERNING AGENCY.
- CONTRACTOR TO CALL 811 FOR UTILITY LOCATES BEFORE DIGGING.
- ALL TRENCHING WITHIN PAVED OR HANDSCAPED AREAS SHALL RECEIVE CLEAN SAWCUTS.
- CONTRACTOR IS RESPONSIBLE FOR TEMPORARY SHORING AND FALSE WORK.

- CONTRACTOR SHALL REPAIR AND ALL DAMAGE CAUSED BY CONSTRUCTION BACK TO EXISTING OR BETTER CONDITION, INCLUDING BUT NOT LIMITED TO IRRIGATION, LANDSCAPE, HARDSCAPE, PAVEMENT, CURBING, ABOVE GRADE EQUIPMENT AND EQUIPMENT PADS, EXISTING UTILITIES (BOTH SHOWN AND NOT SHOWN ON DRAWINGS).
- CONTRACTOR MAINTAIN VERTICAL AND HORIZONTAL SEPARATION AT ALL CROSSING PER THE VA STANDARD SPECIFICATIONS.
- CONTRACTOR IS RESPONSIBLE FOR ANY AND ALL FALSEWORK, STABILIZATION, SHORING, ETC. DURING EXCAVATION AND TRENCHING TO ENSURE ALL EXISTING IMPROVEMENTS AND FACILITIES ARE SECURE AND STABILIZED.
- REFER TO SHEET G-002 FOR PHASING NOTES

Point Table					Point Table					Point Table				
Point #	Raw Description	Elevation	Northing	Easting	Point #	Raw Description	Elevation	Northing	Easting	Point #	Raw Description	Elevation	Northing	Easting
1	001	681.000	505487.9735	1821473.4802	23	021	679.435	505486.6869	1821527.4021	43	043	679.440	505456.2024	1821588.8904
2	002	681.100	505485.8648	1821467.0649	24	024	679.750	505475.5679	1821534.5186	44	044	679.240	505436.2394	1821585.6435
3	003	681.300	505476.5844	1821472.7029	25	025	679.750	505451.3183	1821549.1559	45	045	679.460	505440.8772	1821598.3241
4	004	681.350	505464.8746	1821480.3265	26	026	679.650	505456.8566	1821558.1864	46	046	679.440	505426.6407	1821606.5601
5	005	681.200	505479.5321	1821478.6547	27	027	679.520	505433.1034	1821572.5456	47	047	679.380	505415.8995	1821613.4704
6	006	681.250	505468.0990	1821485.6828	28	028	679.460	505430.3268	1821567.6907	48	048	679.240	505401.6630	1821622.5346
7	007	681.500	505464.8780	1821495.5826	29	029	679.550	505416.2764	1821576.3461	49	049	679.190	505394.2784	1821626.7109
8	008	681.400	505459.5114	1821483.5035	30	030	679.550	505425.1037	1821570.9070	50	050	679.060	505381.5516	1821634.5180
9	009	683.000	505430.7568	1821516.7906	31	031	679.420	505427.9636	1821575.9496	51	051	679.070	505366.5009	1821643.9794
10	010	682.500	505414.3285	1821528.5375	32	032	679.650	505411.0130	1821579.5885	52	052	678.850	505351.3248	1821653.5769
11	011	683.000	505393.0142	1821541.7493	33	033	679.550	505414.0181	1821584.4201	53	053	679.350	505346.7514	1821658.6244
12	012	683.000	505383.0007	1821530.8752	34	034	679.380	505390.5284	1821598.3597	54	054	678.720	505361.7088	1821632.2501
13	013	682.000	505391.7364	1821530.7910	35	035	679.550	505387.3469	1821593.2676	55	055	679.400	505420.0357	1821596.3692
14	014	681.300	505450.7041	1821493.7595	36	036	679.450	505368.9947	1821598.7511	56	056	679.300	505463.6431	1821570.0471
15	015	681.400	505448.5440	1821490.2743	37	037	679.400	505370.9995	1821602.6762					
16	016	682.000	505368.1193	1821556.9731	38	038	679.200	505349.4460	1821612.4493					
17	017	682.000	505329.1084	1821579.6826	39	039	679.250	505325.0048	1821627.7093					
18	017	18.000	505304.4854	1821594.8873	40	040	679.500	505484.2001	1821538.2888					
19	019	680.000	505307.2004	1821581.7118	41	041	679.550	505480.1222	1821556.3723					
20	020	681.000	505333.9047	1821567.4472	42	042	679.460	505479.3287	1821574.9571					

Revisions:	10% BASIS OF DESIGN	Date:
	35% SCHEMATIC DESIGN	08-27-2023
	65% DESIGN DEVELOPMENT	11-08-2023
	95% CONSTRUCTION DOCUMENTS	04-07-2025
		06-12-2025
CONSULTANT		
CONSULTANT:		

CONSULTANT


CONSULTANT:

ARCHITECT/ENGINEER OF RECORD

GDM-AE, Inc.
1308 NE 134TH ST SUITE A
VANCOUVER, WA 98685
P. 541.428.4723
WILL GORDON, CEO
WWW.GDM-AE.COM



STAMP

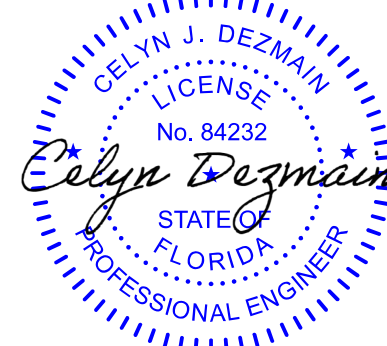

PROGRAM
CONTRACTING
ACTIVITY
CENTRAL (PCAC)



U.S. Department
of Veterans Affairs

DRAWING TITLE

BUILDING 18 - CIVIL GRADING PLAN

APPROVED:

FOR OFFICIAL USE ONLY (FOUO)

PHASE

100% CONSTRUCTION
DOCUMENTS

FLS

FULLY
SPRINKLERED

PROJECT TITLE

VA CHILLICOTHE (EHRM) ELECTRONIC
HEALTH RECORD MODERNIZATION
INFRASTRUCTURE UPGRADES

LOCATION

17273 STATE ROUTE 104
CHILLICOTHE, OH 45601-9718

ISSUE DATE

07/17/2025

CHECKED BY

CD

DRAWN BY

DT

PROJECT NO.

538-21-705


BUILDING NO.

18

DRAWING NO.

00-CG-101

A

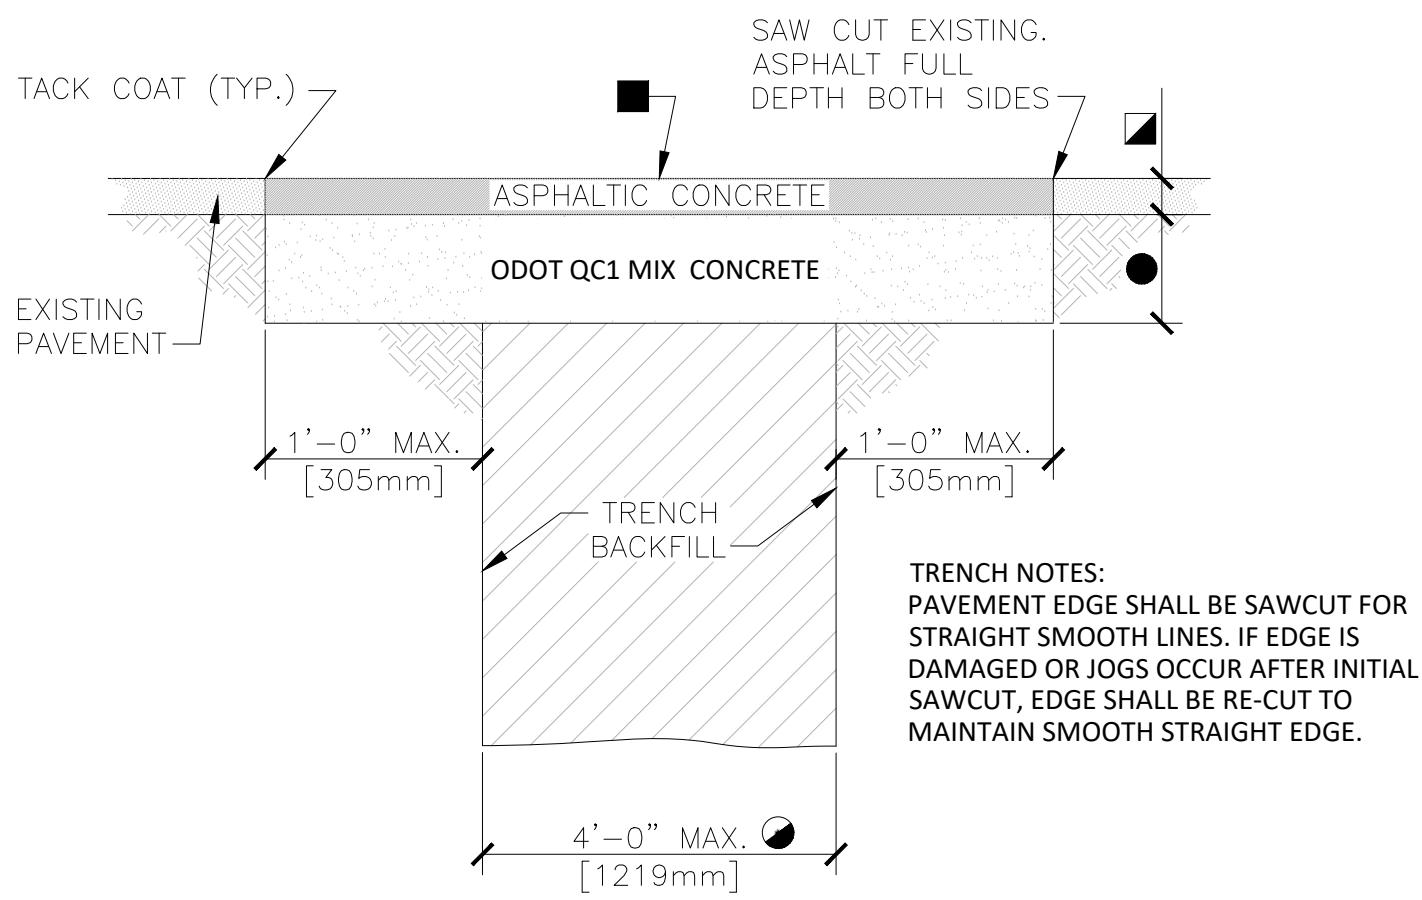


- FOR TRENCH WIDTHS EXCEEDING 4' [1219mm] REFER TO VA STANDARD DETAIL 32 12 16-02 "TYPE 2 UTILITY TRENCH PATCH", FOR TRENCH WHERE PORTLAND CEMENT CONCRETE (PCC) PAVEMENT EXISTS, REFER TO 32 12 16-03 "TYPE 3 UTILITY TRENCH PATCH".
 - 2" [50mm] MINIMUM OR THICKNESS OF EXISTING PAVEMENT WHICHEVER IS GREATER.
 - BITUMINOUS SURFACE TREATMENT (CHIPSEAL) REQUIRED ONLY FOR LONGITUDINAL TRENCHES WITH WIDTHS GREATER THAN 6' [1829mm].
 - 6" MIN THICKNESS OF ODOT QC1 MIX CONCRETE. MIN 28 DAY COMPRESSIVE STRENGTH 4,000 PSI. PROVIDE RELIEF CUTS EVERY 1.5 TIMES THE WIDTH OF TRENCH. PROVIDE RELIEF CUTS AT EVERY ALIGNMENT CHANGE FROM INSIDE CORNER TO OUTSIDE CORNER.
- REFER TO VA STANDARD DETAIL 32 12 16-04 "UTILITY TRENCH PAVEMENT PATCH NOTES" FOR ADDITIONAL INFORMATION.

TYPE 1 UTILITY TRENCH PATCH

01
00-CU-201

NTS

C

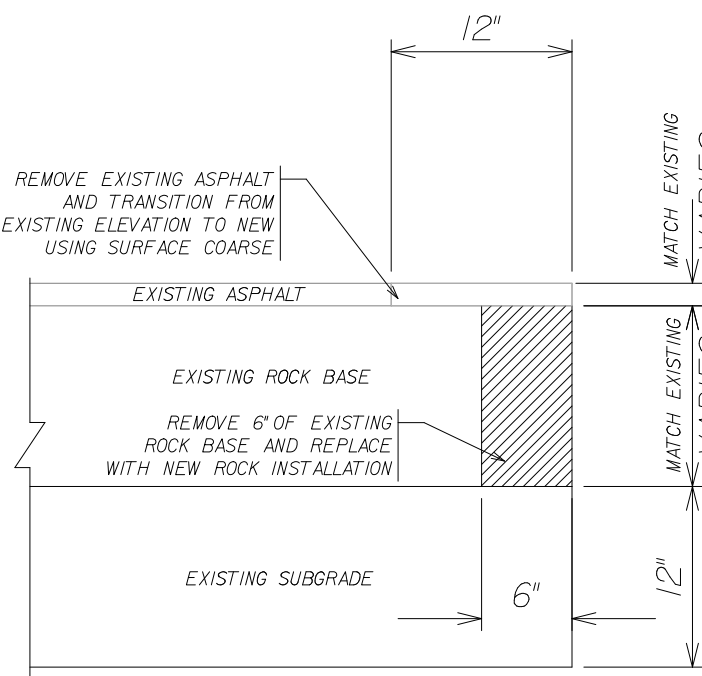


PAVEMENT SAWCUT DETAIL

04
00-CU-201

NTS

D

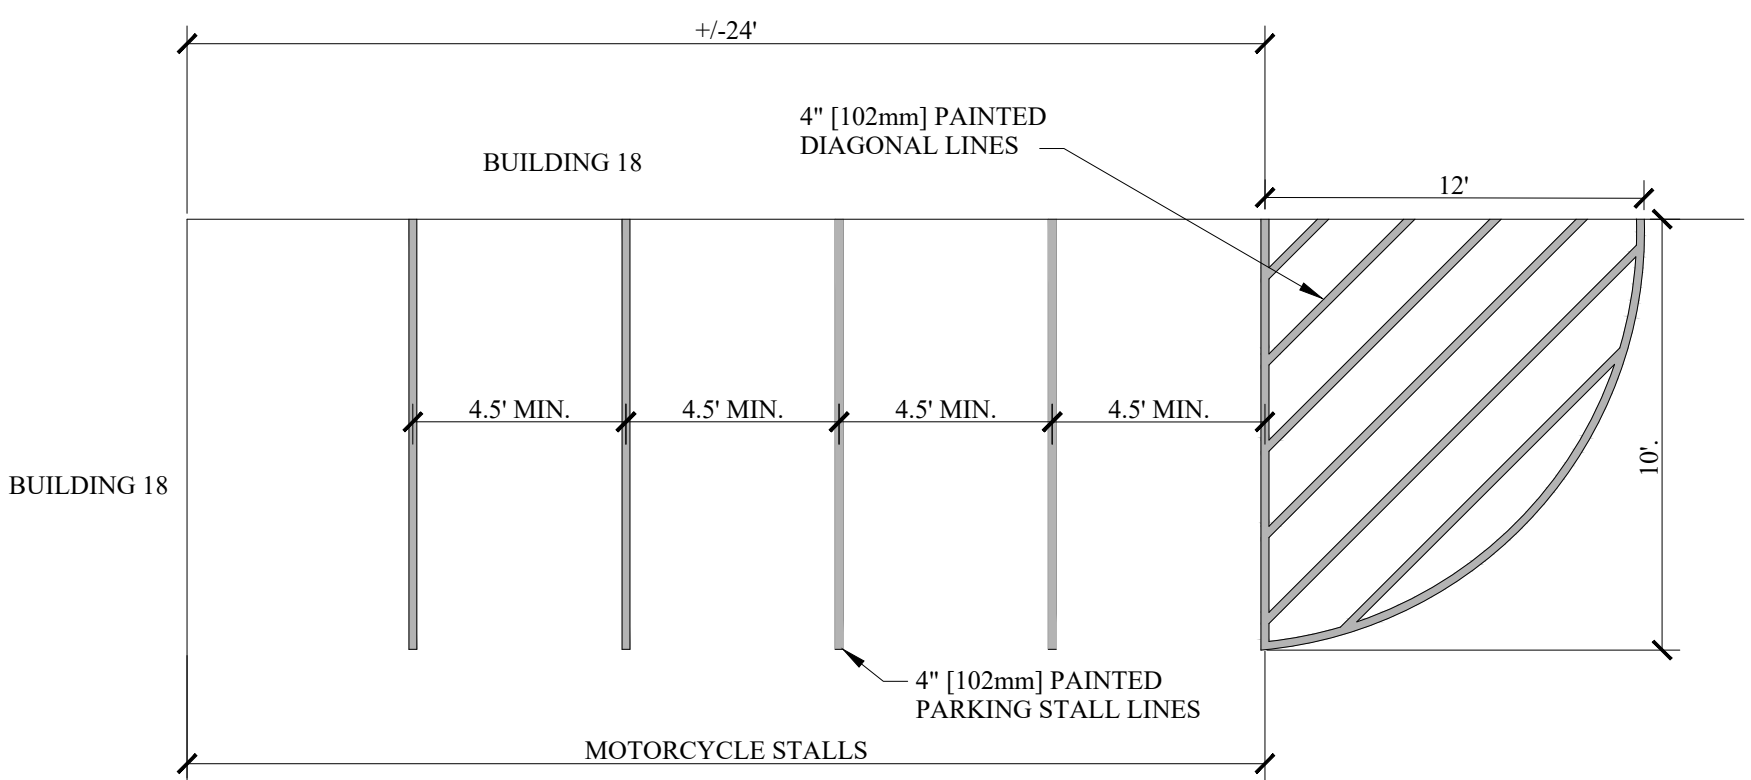

MOTORCYCLE PARKING STALL LAYOUT

07
00-CU-201


NTS

F

GENERAL NOTES

- MATERIAL AND COMPACTION REQUIREMENTS FOR PIPE BEDDING/SHADING SHALL BE IN ACCORDANCE WITH THE SPECIFICATIONS FOR THE APPLICABLE UTILITY PIPE.
 - TRENCH BACKFILL SHALL COMMENCE 1 FOOT [305mm] ABOVE THE TOP OF PIPE AND SHALL BE PER SPECIFICATION 31 20 00.
 - BACKFILL COMPACTION REQUIREMENTS SHALL BE PER SPECIFICATION 31 20 00.
 - THE 1 FOOT [305mm] TRENCH "SHOULDER" AREAS SHALL BE DELETED FOR TYPE 2 TRENCHES.
 - ODOT 304 SHALL BE IN ACCORDANCE WITH THE REQUIREMENTS OF ODOT AND SPECIFICATION 32 12 16.
 - PORTLAND CEMENT CONCRETE SHALL BE IN ACCORDANCE WITH THE REQUIREMENTS OF SPECIFICATION 32 05 23.
 - ASPHALTIC TACK MATERIAL SHALL BE IN ACCORDANCE WITH THE REQUIREMENTS OF ODOT AND VA SPECIFICATION 32 12 16.
 - ASPHALTIC CONCRETE SHALL BE IN ACCORDANCE WITH THE REQUIREMENTS OF ODOT AND VA SPECIFICATION 32 12 16 FOR THE TYPE SPECIFIED.
 - BITUMINOUS SURFACE TREATMENT SHALL BE IN ACCORDANCE WITH THE REQUIREMENTS OF ODOT AND SPECIFICATION 32 12 16 FOR THE TYPE SPECIFIED.
 - LOAD TRANSFER DOWELS FOR JOINTS TRANSVERSE TO THE ROADWAY CENTERLINE SHALL BE SMOOTH STEEL DOWELS IN ACCORDANCE WITH THE REQUIREMENTS OF SPECIFICATION 32 05 23. DOWELS SHALL BE SIZED AND SPACED AS FOLLOWS:
- | PCCP THICKNESS | DOWEL SIZE | DOWEL LENGTH | DOWEL SPACING |
|----------------|--------------|--------------|---------------|
| 6" [150mm] | #5 [No. 16] | 12" [305mm] | 18" [455mm] |
| 7" [180mm] | #6 [No. 19] | 15" [380mm] | 15" [380mm] |
| 8" [180mm] | #8 [No. 19] | 15" [380mm] | 12" [305mm] |
| 10" [180mm] | #10 [No. 19] | 15" [380mm] | 12" [305mm] |
- DEFORMED TIE BARS SHALL BE USED IN TRENCH PATCHES LONGITUDINAL TO THE ROADWAY CENTERLINE WHEN THE TRENCH LENGTH IS GREATER THAN 50 FEET [15240mm]. TIE BARS SHALL BE 24 INCHES [610mm] LONG, DEFORMED #4 [No. 13] BARS FOR PCCP LESS THAN 8 INCHES [205mm] THICK AND #5 [No. 16] BARS IF 8 INCHES [205mm] THICK OR MORE. TIE BARS SHALL BE PLACED 30 INCHES [760mm] CENTER-TO-CENTER.
 - HOLES SHALL BE DRILLED 1 FOOT [305mm] INTO THE EXISTING SLAB FOR TIE BARS AND 7 INCHES [180mm] FOR DOWELS. HOLES SHALL BE OF A DIAMETER SUFFICIENT TO ACCOMMODATE THE TIE BAR ANCHORAGE OR DOWEL CAP. TIE BARS SHALL BE ANCHORED WITH AN APPROVED HIGH VISCOSITY EPOXY.
 - IF THE CONCRETE SLAB REMAINING NEXT TO A LONGITUDINAL OR TRANSVERSE JOINT IS LESS THAN 6 FEET [1829mm] AT ITS NARROWEST WIDTH, REMOVE AND REPLACE THE EXISTING CONCRETE TO THE JOINT.
 - EXISTING BURIED DEBRIS INCLUDING BUT NOT LIMITED TO CONCRETE RUBBLE, BUILDING MATERIALS, TRASH, MAY BE PRESENT DURING EXCAVATION. CONTRACTOR IS RESPONSIBLE FOR REMOVING DEBRIS WITHIN TRENCHING LIMITS IF ENCOUNTERED TO MAINTAIN HORIZONTAL AND VERTICAL SEPARATION AND BURY DEPTH REQUIREMENTS.

PCCP THICKNESS	DOWEL SIZE	DOWEL LENGTH	DOWEL SPACING
6" [150mm]	#5 [No. 16]	12" [305mm]	18" [455mm]
7" [180mm]	#6 [No. 19]	15" [380mm]	15" [380mm]
8" [180mm]	#8 [No. 19]	15" [380mm]	12" [305mm]
10" [180mm]	#10 [No. 19]	15" [380mm]	12" [305mm]

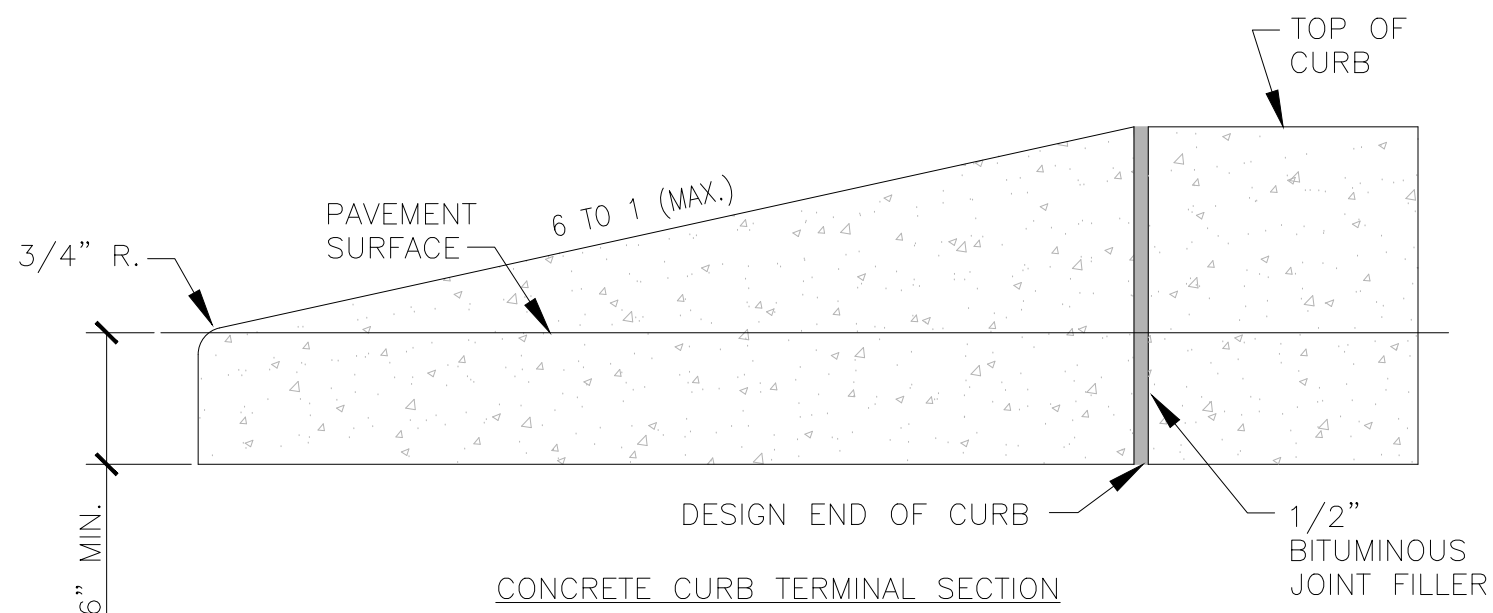

NOTES:

- ALL CONCRETE CURBS AND TRANSITIONS, SHALL BE ODOT ITEM 452 - QC1 MIX WITH SYNTHETIC FIBER REINFORCEMENT AT 3/4 LB/CY (±1/4 LB/CY)
- MAXIMUM SPACING ON SCORED JOINTS SHALL BE 15' OR EQUAL TO ADJACENT SIDEWALK.
- 1/2" THICK EXPANSION JOINTS SHALL BE LOCATED AT TRANSITIONS (ELEVATION OR MATERIAL), CHANGES IN DIRECTION OF CURB RETURNS (CURVES), AND AT A MAXIMUM OF 60' INTERVALS. EXPANSION MATERIAL SHALL ALSO BE PLACED BETWEEN CURBS AND ADJACENT STRUCTURES, SIDEWALKS, DRIVEWAYS AND CURB ACCESS RAMPS. THE 1/2" JOINT FILLER SHALL EXTEND THE FULL DEPTH OF THE CONCRETE. JOINTS ABUTTING EXISTING ASPHALT, CURB, OR SIDEWALK SHALL BE SAW CUT FLUSH.
- CONCRETE SHALL BE FINISHED WITH A STEEL TROWEL FOLLOWED BY BRUSHING WITH A FINE BRUSH ALONG THE LENGTH OF THE CURB OR CURB AND GUTTER.
- SINGLE CURB MAY BE CONSTRUCTED BY THE USE OF FORMS OR MAY BE SLIP FORMED.
- ALL EXPOSED EDGES AND HAND TOOLED JOINTS SHALL BE FINISHED WITH A TOOL HAVING A 1/4" RADIUS UNLESS A LARGER RADIUS IS INDICATED BY THE APPLICABLE STANDARD DETAIL OR PROJECT PLANS.
- FOR REVEALS OF 6" TO LESS THAN 8".
- FOR REVEALS OF 8" TO 10".


CONCRETE VERTICAL CURB

02
00-CU-201

CONCRETE CURB AND TERMINAL SECTION

NTS

3" MIN 6" MAX TYPE 1 ASPHALT PAVEMENT
REFER TO PAVEMENT NOTES

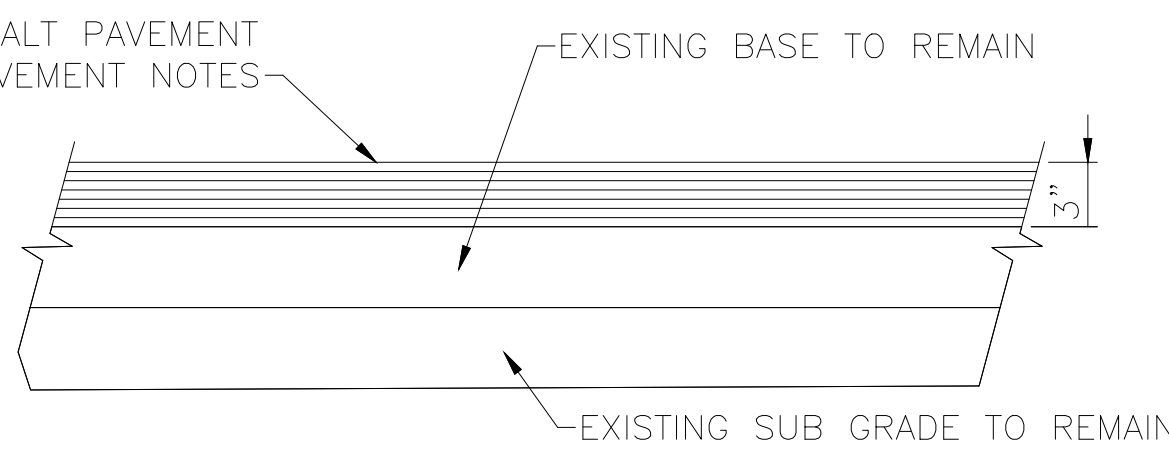

ASPHALTIC PAVEMENT SECTION

03
00-CU-201

NTS

PAVEMENT NOTES:

- EXISTING ASPHALT WAS FOUND TO BE +/- 8" THICK IN SOME LOCATIONS. CONTRACTOR SHALL VERIFY THICKNESS OF EXISTING ASPHALT.
- PAVEMENT SHALL BE TYPE 1 HOT MIX ASPHALTIC CONCRETE (HMAC) IN ACCORDANCE WITH ODOT, MIN 3" THICK AND MAX 6" THICK INSTALLED IN MIN 1.5" LIFTS AND MAX 2" LIFTS. TACK COAT SHALL BE INSTALLED PER SPECIFICATION BETWEEN FIRST AND SECOND LIFT.
- IF FINISHED ELEVATION CAN NOT BE MET WITHIN MAX 6" THICKNESS OF TYPE 1 HMAC, INSTALL TYPE 2 BINDER COURSE AT A MIN 1.5" THICK AS FIRST LIFT. TACK COAT SHALL BE INSTALLED BETWEEN FIRST AND SECOND LIFT IF BINDER COURSE IS NEEDED.
- EXISTING ROCK BASE SHALL NOT BE DISTURBED, HOWEVER IF NEEDED SHALL BE PLACED IN 3 INCH LIFTS. THE LIFTS SHALL BE 0.01 APPROVED BASE ROCK. BASE ROCK SHALL BE PRIMED IN ACCORDANCE WITH OHIO DEPARTMENT OF TRANSPORTATION (O.D.O.T.) STANDARD SPECIFICATIONS AND THE VA SPECIFICATIONS. ALL BASE ROCK SHALL BE COMPACTED TO NOT LESS THAN 98% MAXIMUM DRY DENSITY AS DETERMINED BY A.S.H.T.O. T-99 IF DISTURBED.
- WHERE BASE AND SUBGRADE ARE DISTURBED, EITHER INTENTIONALLY OR UNINTENTIONALLY, DENSITY TESTS SHALL BE CONDUCTED FOR A MAXIMUM 5000 SQUARE FEET OF FINISHED PAVEMENT OR @ 300' INTERVALS MAX ON EACH LANE.
- TACK COAT SHALL BE APPLIED AT A RATE OF 0.25 GALLONS PER SQUARE YARD. TACK COAT FOR BASE SHALL CONFORM TO THE REQUIREMENTS AND SPECIFICATIONS OF THE V.A., ODOT, WHICH EVER IS MORE CONSERVATIVE.
- PROCTOR SHALL BE PERFORMED ON ALL MATERIAL, SUBGRADE AND BASE AND SUBSEQUENT CHANGES IN MATERIAL. BEARING RATIOS, SIEVE ANALYSIS AND DENSITIES REQUIRED BY THE CONTRACT DOCUMENTS SHALL BE SUBMITTED TO THE C.O.R.
- ALL REPAIRS TO EXISTING PAVEMENT SHALL RECEIVE SAW-CUT EDGES PRIOR TO REPAVING ASPHALT.
- MINIMUM LONGITUDINAL SLOPE OF PAVEMENT SHALL BE 0.5%.
- DEMOLISHING SHALL BE IN ACCORDANCE WITH V.A. STANDARD SPECIFICATIONS OR AS DIRECTED BY GEOTECHNICAL ENGINEER.
- ALL ABOVE GRADE IMPROVEMENTS WITHIN PAVED SURFACES SHALL RECEIVE SAWCUTS AND EXISTING PAVEMENT REMOVED.
- CONTRACTOR SHALL RESET ALL COVERS, RIMS, LIDS, GRATES ETC. WITHIN PAVED AREA TO MATCH NEW PROPOSED FINISH ELEVATION.
- PAVING SEAMS SHALL BE FLUSH, WITH A 1/4" TOLERANCE, AND SHALL BE LOCATED AT THE EDGE OF A LANE.
- WHERE TRENCHING OCCURS WITHIN LIMITS OF NEW PAVING SCOPE, THE TRENCH SHALL FOLLOW DETAIL 01/00-CU-201. THE CONCRETE BASE SHALL BE POURED TO MEET THE BOTTOM OF THE FINAL PAVEMENT LIFT TO ALLOW A CONTINUOUS FINAL LIFT WITHOUT TRENCH/PATCH SEAMS.

A

B

C

D

E

F

A

B

C

D

E

F

A


B

C


D

E



F

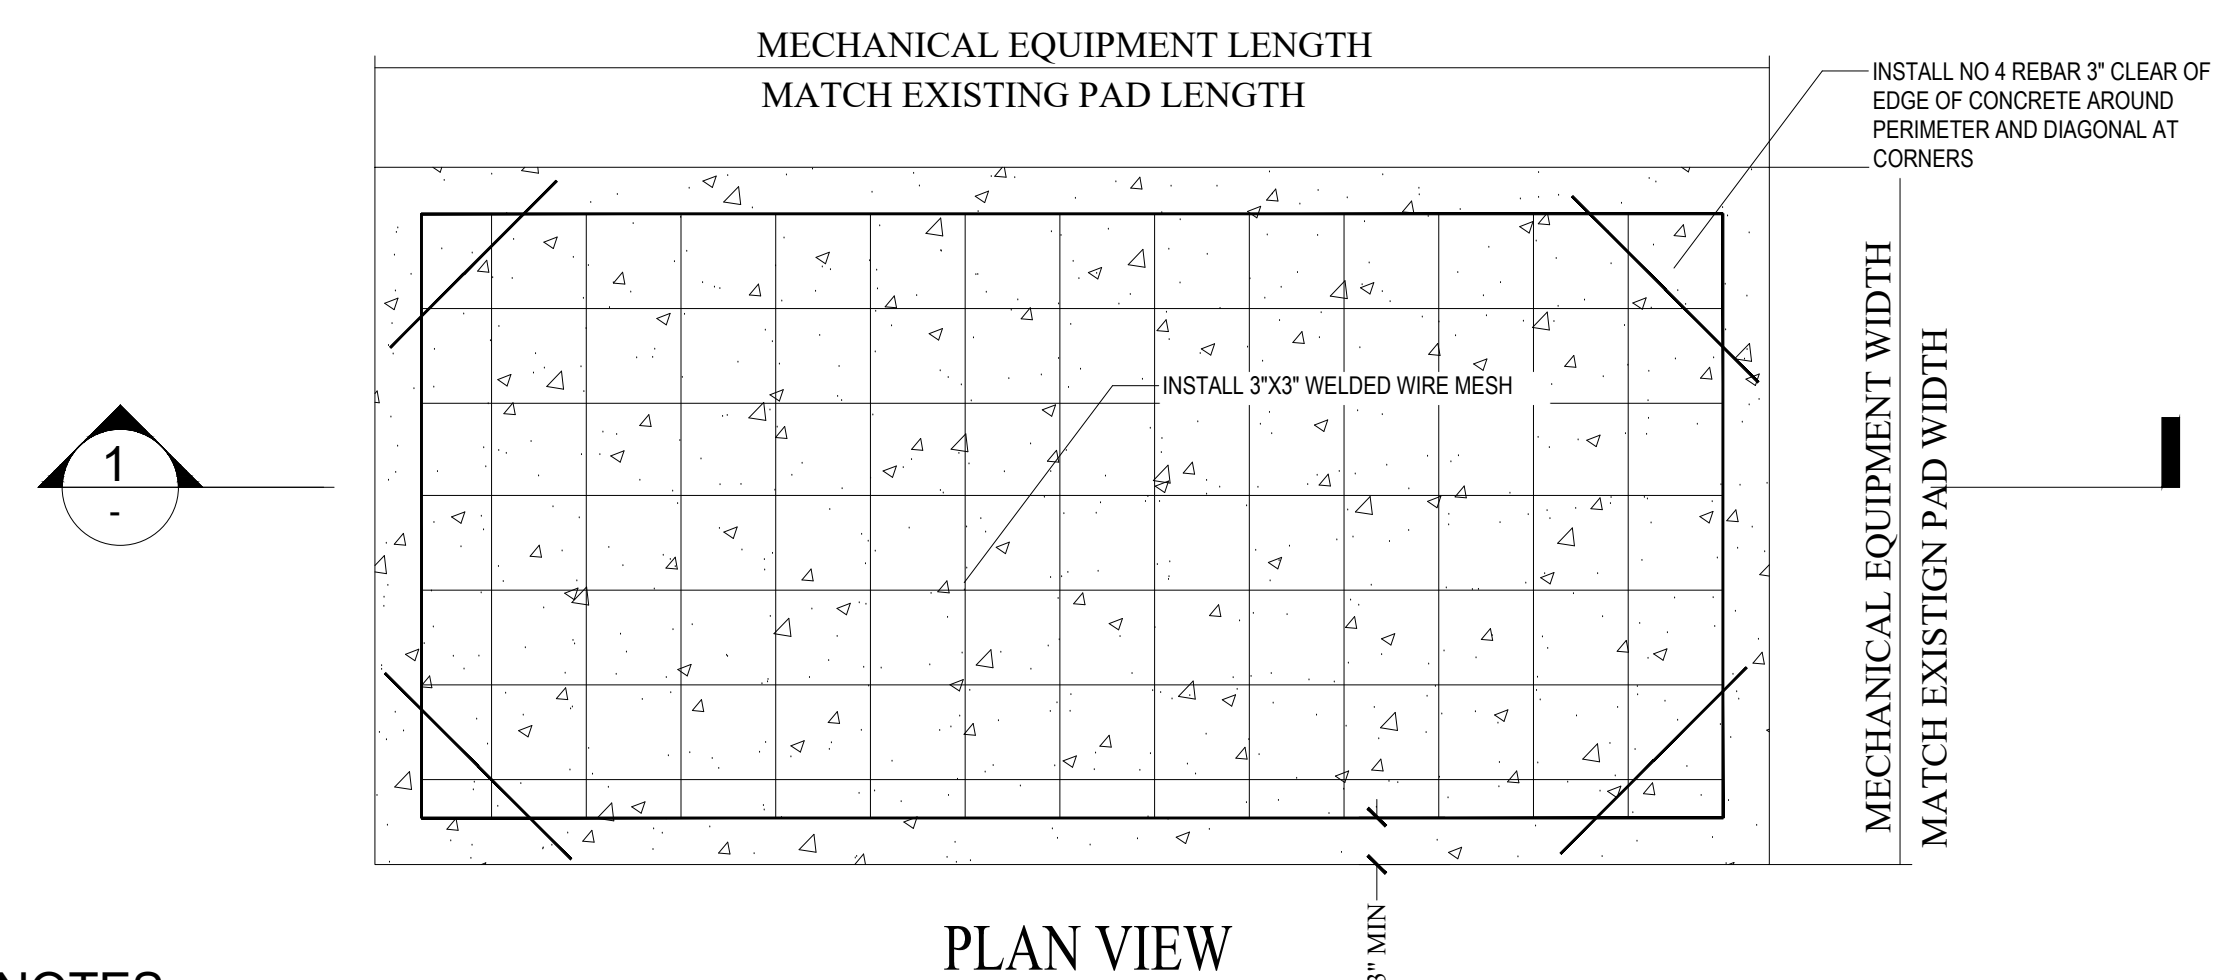

- NOTES:**
1. PROVIDE FALSE WORK AND SHORING AS REQUIRED FOR NEW AND EXISTING MATERIALS.
 2. EQUALLY SPACED CONTROL JOINTS REQUIRED IF SURFACE IS GREATER THAN 100 SQUARE FEET.
 3. 500 POUNDS MAXIMUM ALLOWABLE EQUIPMENT WEIGHT.
 4. MINIMUM CONCRETE STRENGTH: 3500 PSI @ 28 DAYS.
 5. MINIMUM CONCRETE COVER OF 3".
 6. REFER TO MECHANICAL PLANS FOR HORIZONTAL CLEARANCE AND ORIENTATION REQUIRED FOR EQUIPMENT.
 7. REFER TO MECHANICAL PLANS FOR EQUIPMENT SIZING.
 8. SUBGRADE SHALL BE CLEAN NATIVE FILL COMPACTED TO 95% MAXIMUM DRY DENSITY. NO ORGANIC MATERIAL SHALL BE ALLOWED.

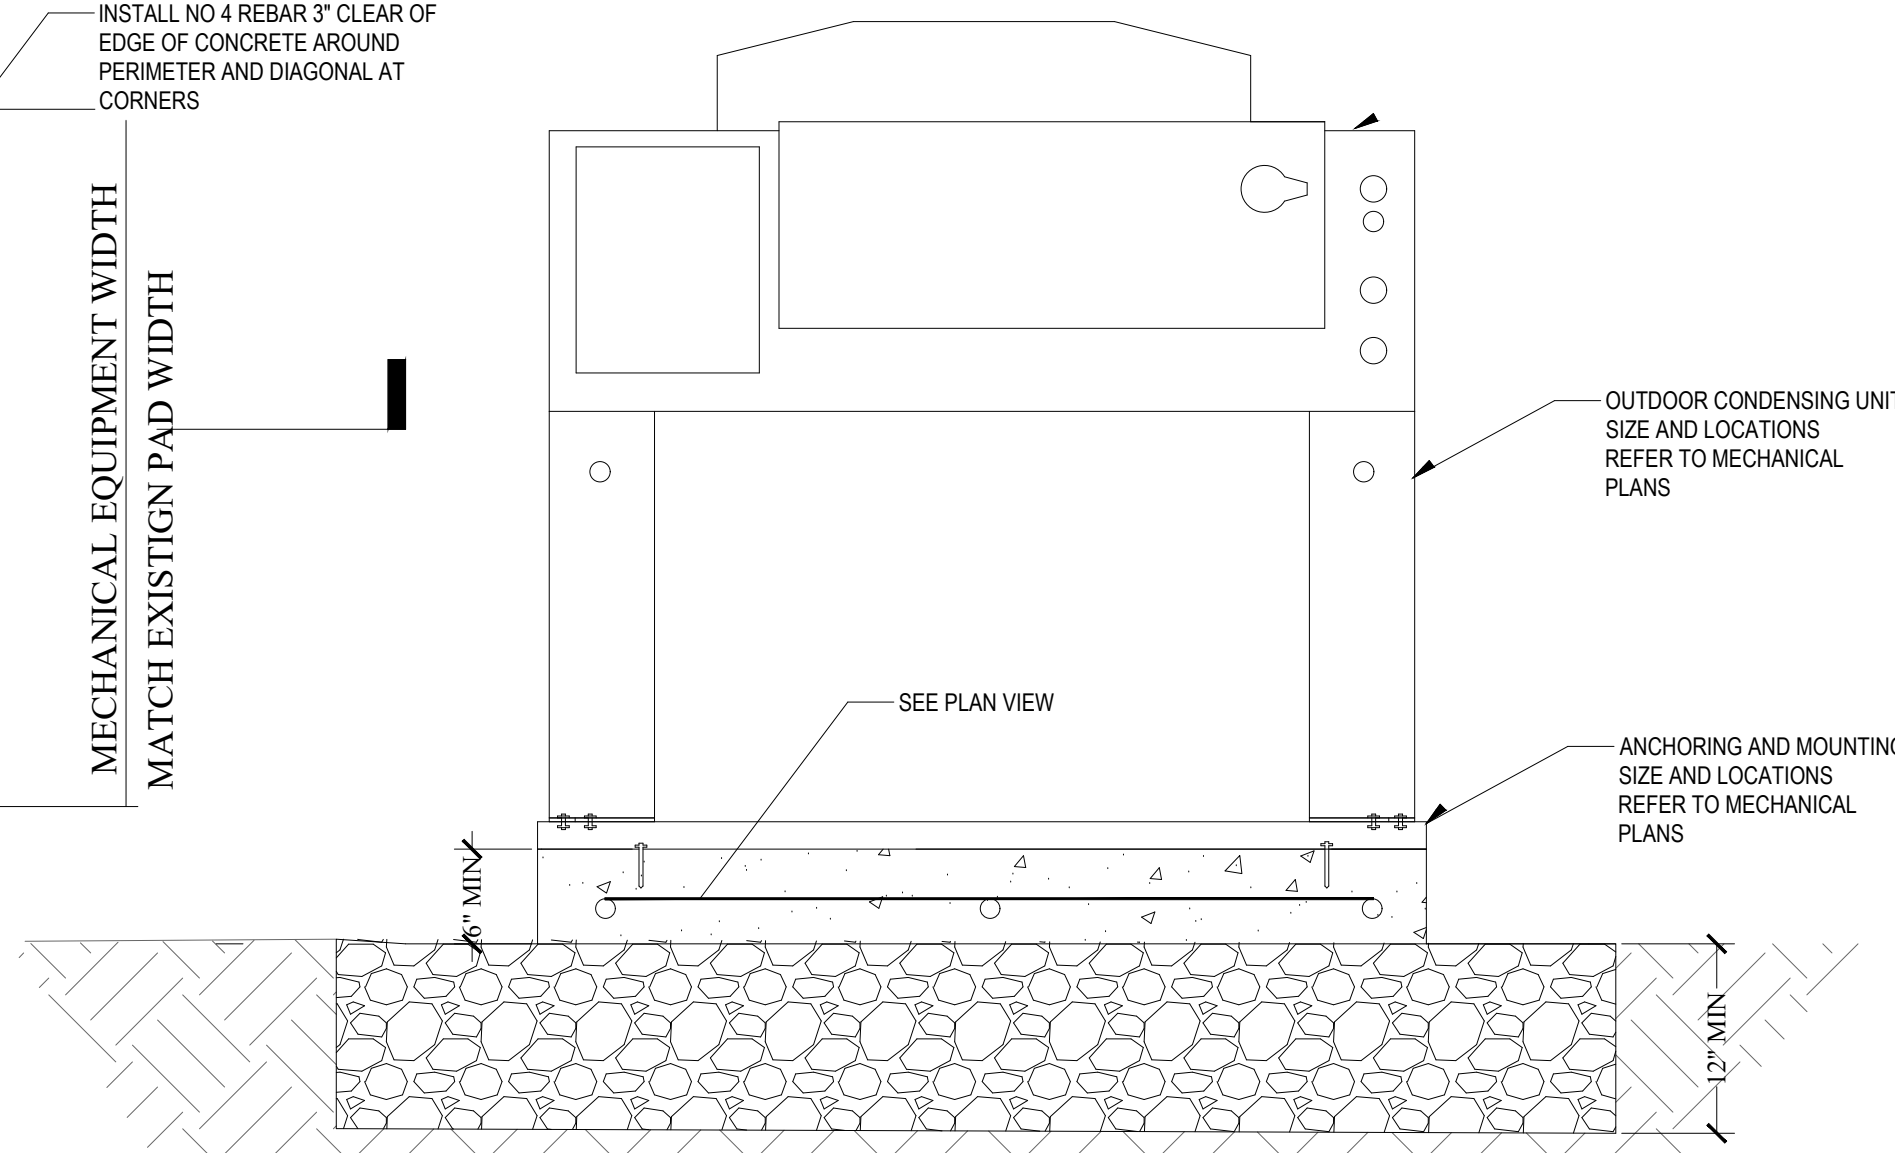

01
00-CU-202
NTS
OUTDOOR MECHANICAL EQUIPMENT FOUNDATION PAD DETAIL

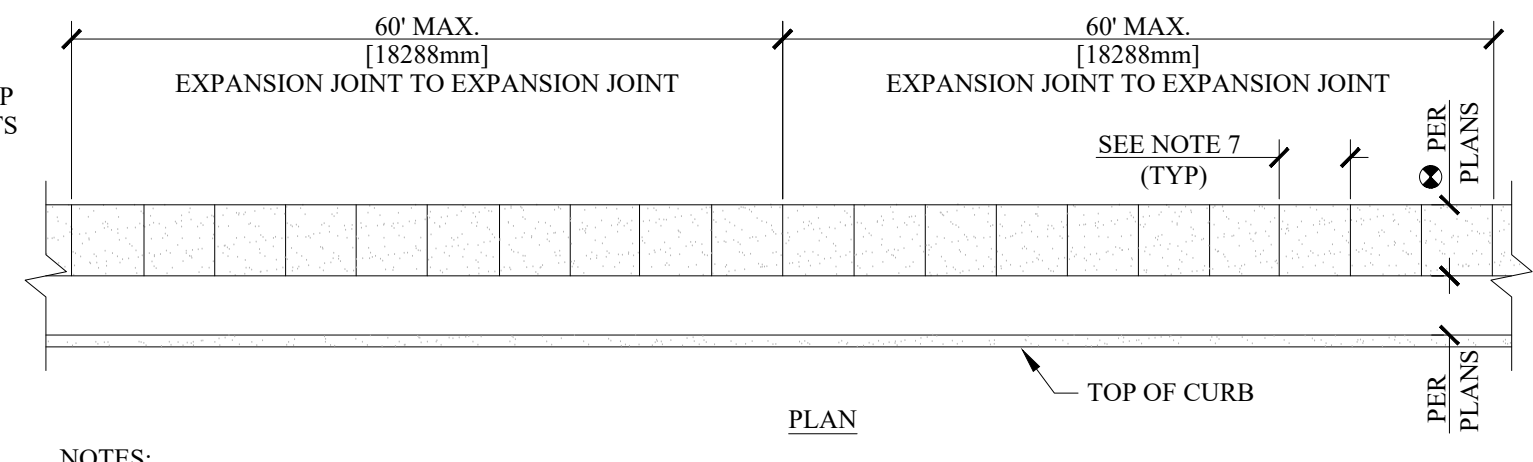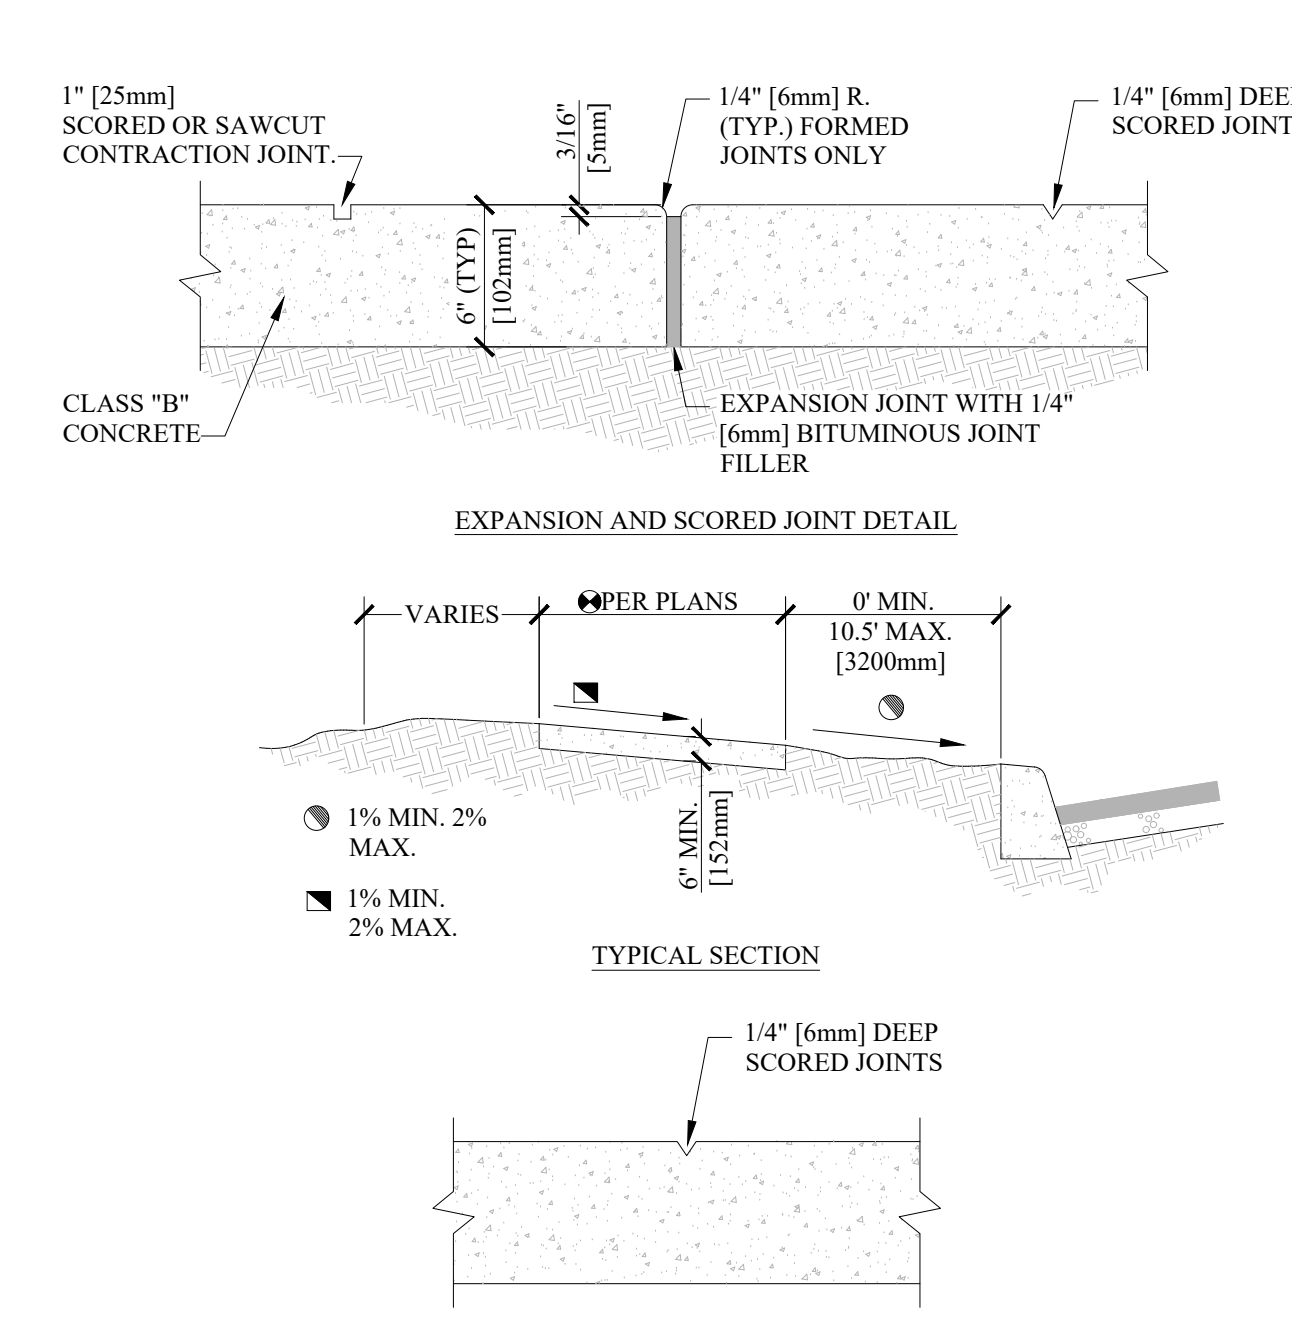


- NOTES:**
1. EXPANSION JOINTS SHALL BE LOCATED WHERE SIDEWALK ABUTS CONCRETE DRIVEWAYS, CURB OR OTHER ADJACENT STRUCTURES.
 2. ONE-HALF INCH BITUMINOUS JOINT FILLER SHALL BE INSTALLED AT EXPANSION JOINT LOCATIONS AND SHALL EXTEND THE FULL DEPTH OF THE CONCRETE.
 3. 1" DEEP CONTRACTION JOINTS SHALL BE PLACED AT INTERVALS OF APPROXIMATELY 15' [4572mm] OR AT A SPACING THAT MATCHES THE ADJACENT CURB.
 4. FORMED CONTRACTION JOINTS SHALL BE FINISHED WITH A TOOL HAVING A 1/4" [6mm] RADIUS.
 5. SCORED JOINTS SHALL BE 1/4" [6mm] DEEP AND PLACED AT THE SPACING INDICATED FOR THE WIDTH OF SIDEWALK OR MATCH SCORED JOINTS OF ADJACENT CURB.
 6. CONCRETE SHALL BE FINISHED BY MEANS OF A FLOAT, STEEL TROWELLED AND BROOMED WITH A FINE BRUSH IN A TRANSVERSE DIRECTION.
 7. 1/4" DEEP SCORED JOINTS (TYP) SPACED AT 6' [1829mm] OR EQUAL TO SIDEWALK WIDTH.

CONTROL JOINT

02
00-CU-202
NTS
CONCRETE SIDEWALK

12" ROUND GRATE

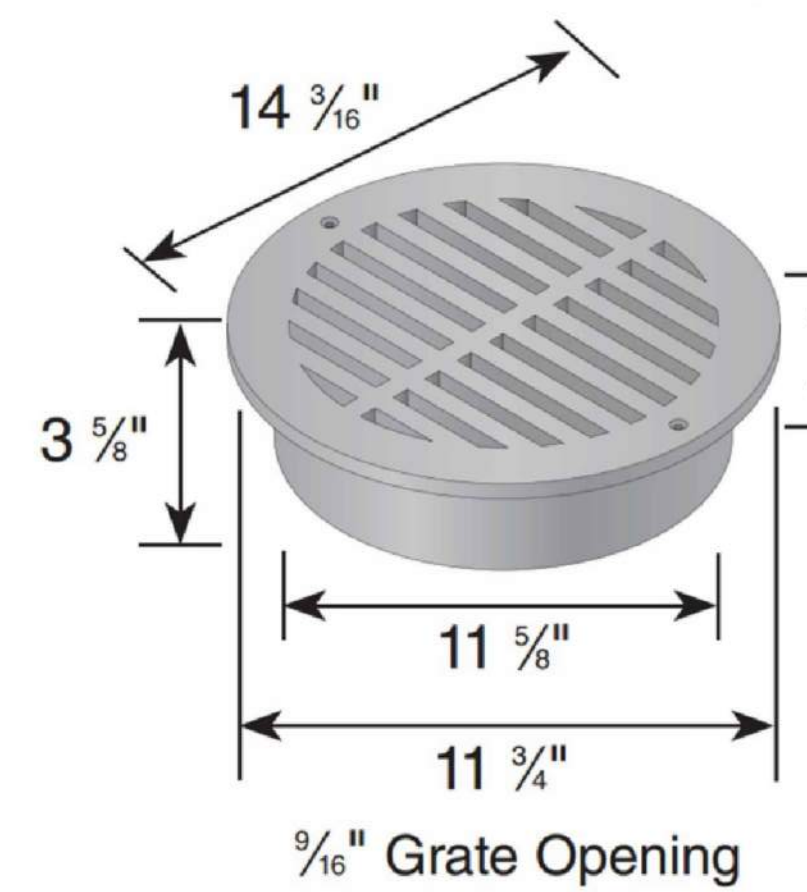


Material: UV Protected High Density Polyethylene (HDPE)
Colors: Black (1240), Green (1250), Gray (1260)
Weight: 2.66 lbs
Fits: 12" SDR-35, Corrugated, SCH-40, Class 125, & Double wall pipes
Grate Openings: 46.00 in² open space
Will accommodate 140.72 gallons per minute with 1/2" of head.

Load Recommendation Guide

Class B


- Loads of 61-175 psi.
- Recommended for medium-duty pneumatic tire traffic, autos and light trucks at speeds less than 20 m.p.h.

Note: Some installations may require a concrete collar to meet head rating. Loads are based on prevailing practice for concrete. Product must be installed using HDS instructions.

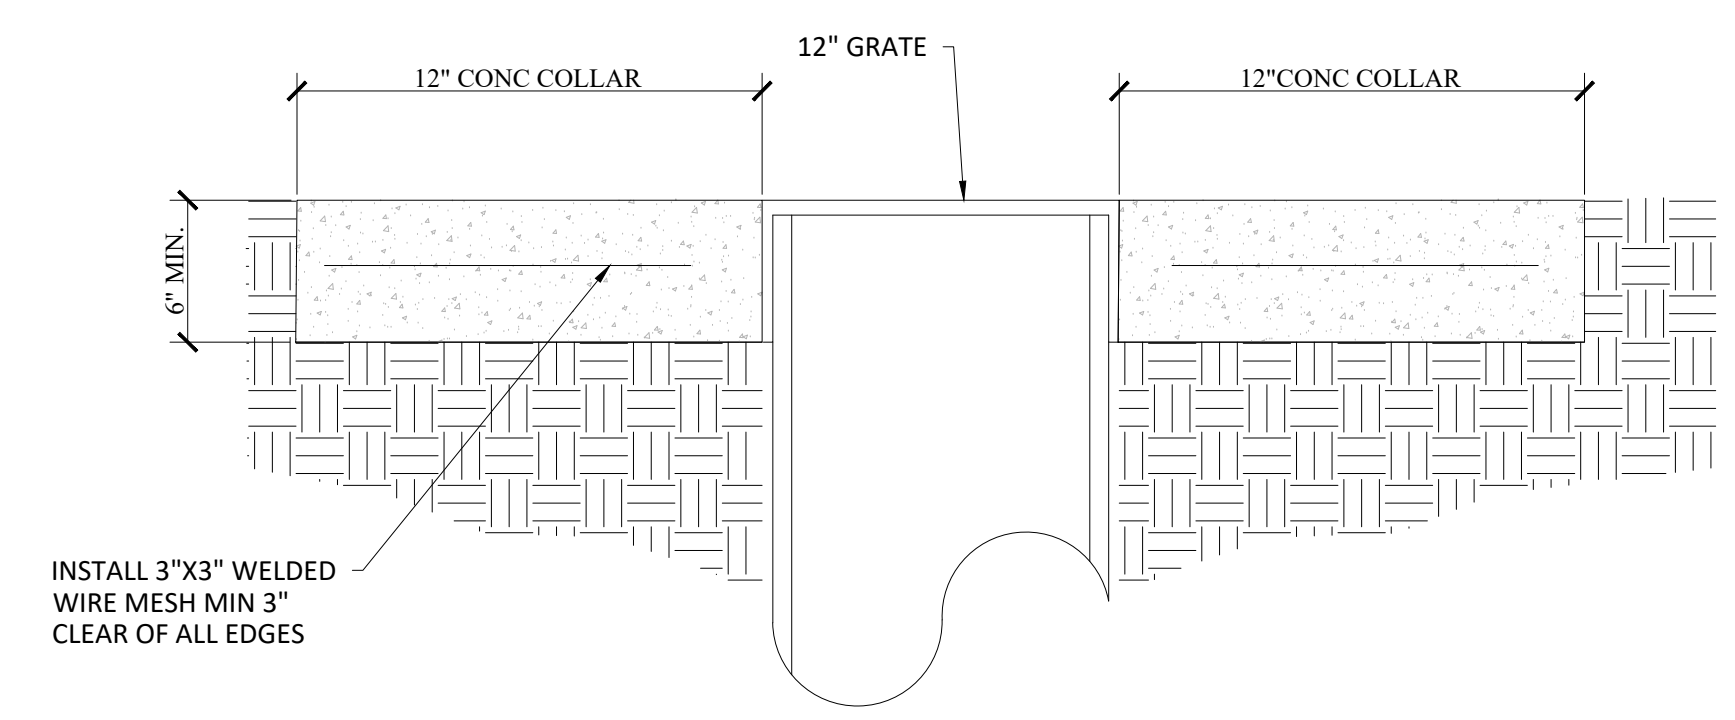


- NOTES:**
1. CONTRACTOR SHALL FORM CONCRETE COLLAR MIN 12" OFFSET FROM EDGE OF GRATE AROUND ENTIRE PERIMETER.
 2. GRATE SHALL BE MEDIUM DUTY.
 3. CONCRETE SHALL BE 3,000 PSI AT 28 DAYS MIN.
 4. CONCRETE SHALL BE BROOM FINISHED SMOOTH.

06
00-CU-202
NTS
GRATE AND COLLAR DETAIL

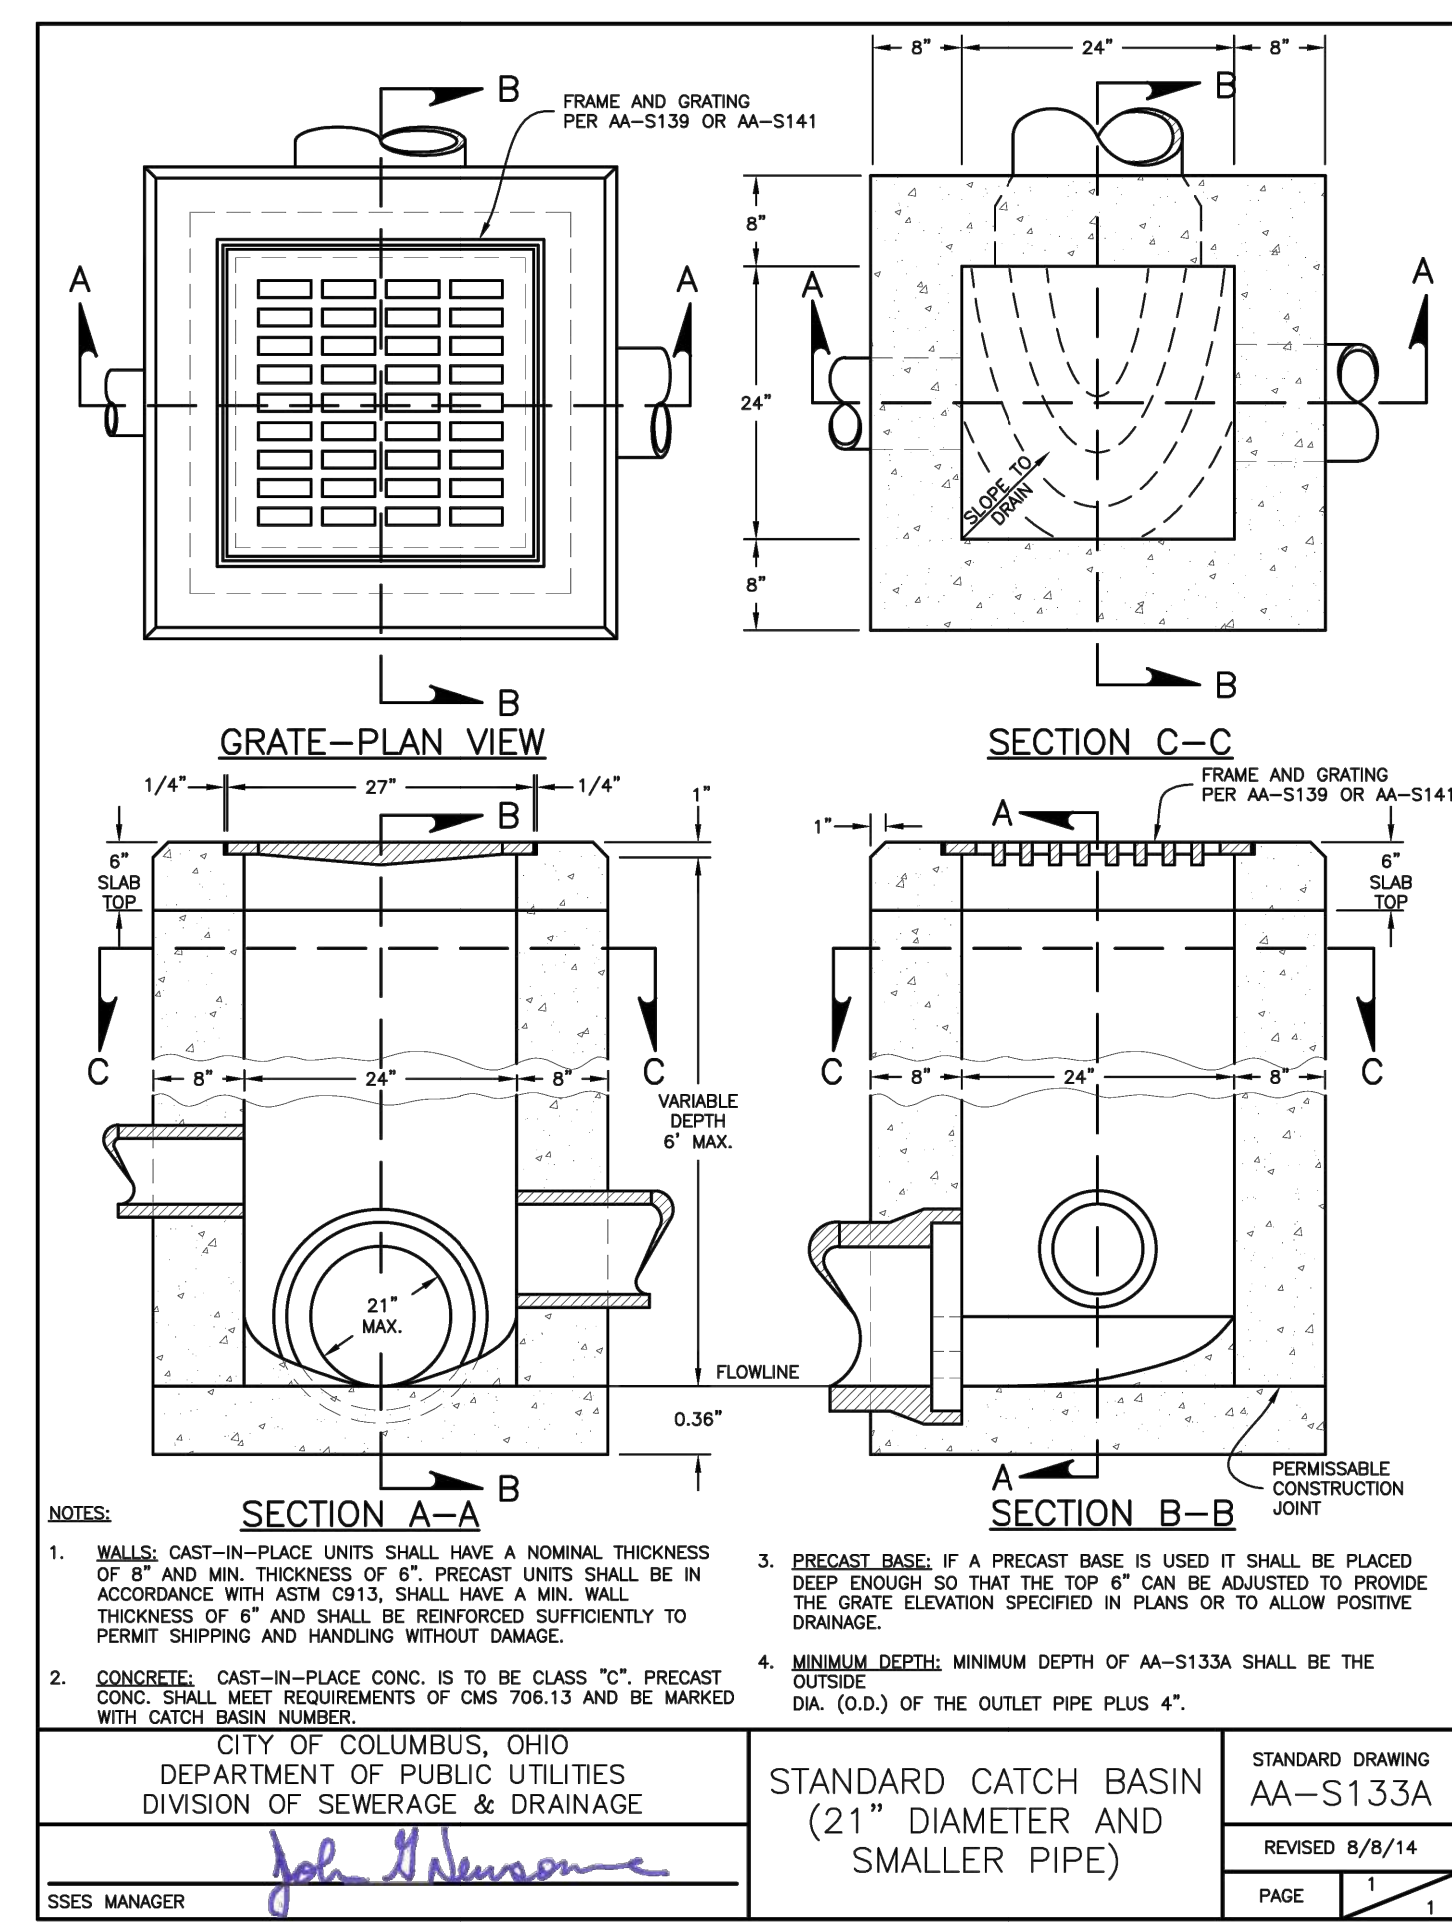


04
00-CU-202
NTS
CATCH BASIN DETAIL

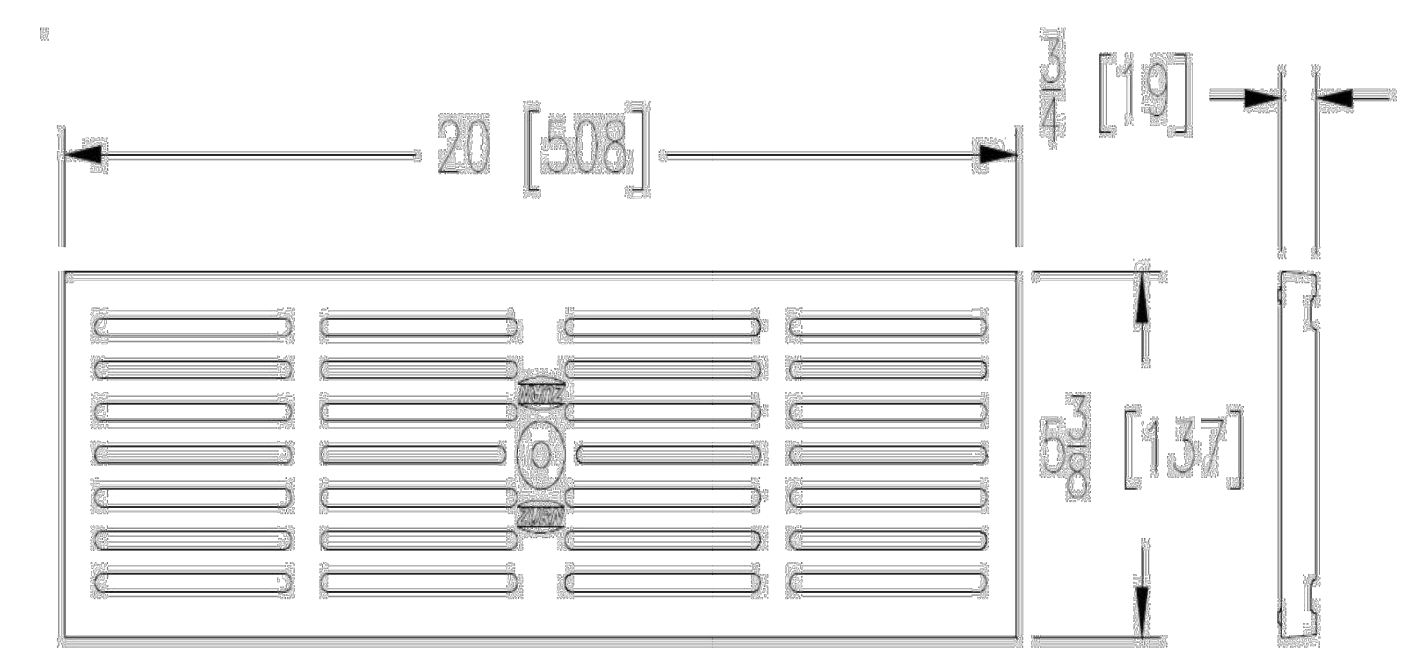

Specification

Heel-Proof Slotted, Ductile Iron grate, is 5-3/8 inches wide by 20 inches long, weighing 6.3 lbs per linear foot. The grate has an open area of 17.0 square inches per linear foot, DIN Rating of B, ANSI Rating of Medium-Duty, ADA compliant. Supplied by Trench Drain Supply.

HPD - Heel-Proof Slotted	
Material:	Ductile Iron
DIN Rating:	Class B
Weight:	6.3 lbs/ft.
Open Area:	17.0 in ² /ft.
ANSI Rating:	Medium-Duty
Application:	Heel-Proof
Slot Width/Hole Size:	1/4"
ADA:	Yes
H-20:	No
FAA:	No

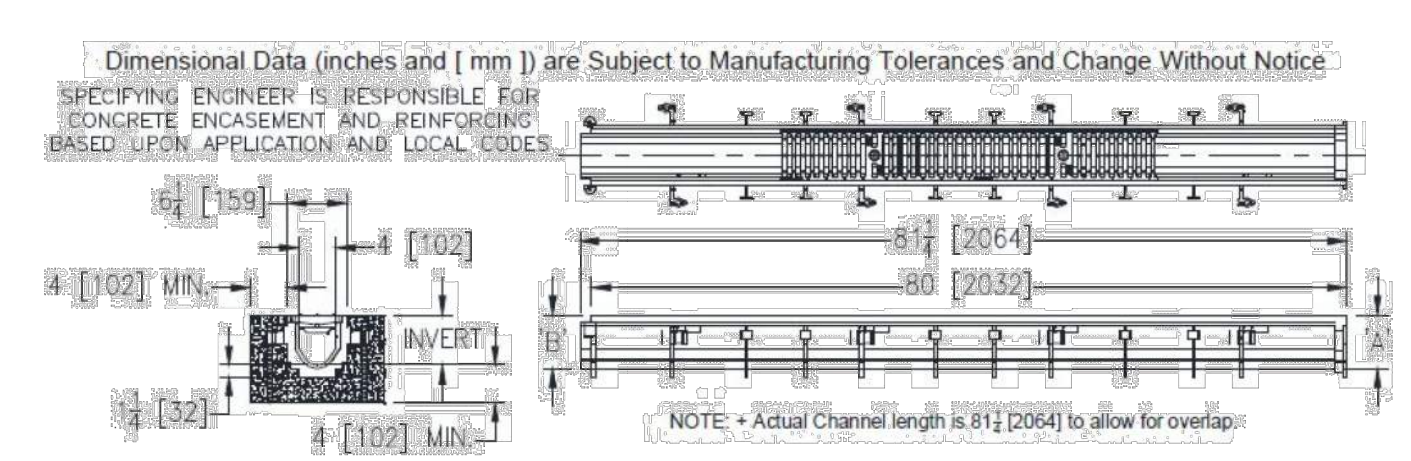

Trench No.	Shallow Inv.	Deep Inv.	(cfs)	(gpm)	(lps)
8601	3.50 [89]	4.10 [104]	0.21	93	6
8602	4.10 [104]	4.70 [119]	0.27	122	9
8603	4.70 [119]	5.30 [135]	0.34	152	10
8603N	5.30 [135]	5.90 [150]	0.41	183	12
8604	5.90 [150]	6.50 [165]	0.48	214	13
8605	6.50 [165]	7.10 [180]	0.55	245	15
8606N	7.10 [180]	7.70 [195]	0.62	276	17
8607	7.70 [195]	8.30 [211]	0.69	308	19
8608	8.30 [211]	8.90 [226]	0.76	339	21
8610	8.90 [226]	9.50 [241]	0.83	371	23
8611	9.50 [241]	10.10 [257]	0.90	403	25
8612	10.10 [257]	10.70 [272]	0.97	435	27
8612N	10.70 [272]	11.30 [287]	1.04	467	29
8613	11.30 [287]	11.90 [302]	1.11	498	31
8614	11.90 [302]	12.50 [318]	1.18	530	33

- NOTES:**
1. CONTRACTOR SHALL PROVIDE TRENCH DRAIN OR APPROVED EQUAL.
 2. GRATE SHALL BE MEDIUM DUTY AND ADA COMPLIANT.
 3. TRENCH SHALL MAINTAIN POSITIVE SLOPE TOWARD INVERT.

05
00-CU-202
NTS
TRENCH DRAIN DETAIL

Revisions: 10% BASIS OF DESIGN 35% SCHEMATIC DESIGN 65% DESIGN DEVELOPMENT 95% CONSTRUCTION DOCUMENTS	Date: 08-27-2023 11-08-2023 04-07-2025 06-12-2025	CONSULTANT CONSULTANT:	ARCHITECT/ENGINEER OF RECORD GDM-AE, Inc. 1308 NE 134TH ST SUITE A VANCOUVER, WA 98685 P: 541-426-4723 WILL GORDON, CEO WWW.GDM-AE.COM	STAMP GDM ARCHITECTS • ENGINEERS	PROGRAM CONTRACTING ACTIVITY CENTRAL (PCAC) VA U.S. Department of Veterans Affairs	DRAWING TITLE CIVIL - DETAILS APPROVED: FOR OFFICIAL USE ONLY (FOUO)	PHASE 100% CONSTRUCTION DOCUMENTS FLS FULLY SPRINKLERED	PROJECT TITLE VA CHILlicothe (EHRM) ELECTRONIC HEALTH RECORD MODERNIZATION INFRASTRUCTURE UPGRADES LOCATION 17273 STATE ROUTE 104 CHILlicothe, OH 45601-9718 ISSUE DATE 07/17/2025 CHECKED BY CD DRAWN BY DT	PROJECT NO. 538-21-705 BUILDING NO. 18 DRAWING NO. 00-CU-202
--	--	----------------------------------	---	---	--	--	---	---	---



GRAPHIC	DESCRIPTION	PRIORITY
	NEW CONSTRUCTION	
	EXISTING PARTITION	
	TO BE DEMOLISHED	
	2 HR SMOKE / FIRE	1
	2 HR SHAFT	2
	2 HR FIRE	3
	1 HR SMOKE / FIRE	4
	1 HR FIRE	5
	HAZARDOUS	6
	NON RATED PARTITION	7

018-AD-111




 GYP. BD. CEILING SYSTEM

 2 X 2 ACOUSTICAL LAY-IN CEILING SYSTEM.

 DOWN LIGHT FIXTURE

PROJECT NO. 538-21-705
BUILDING NO. 18
DRAWING NO. 018-AD-112

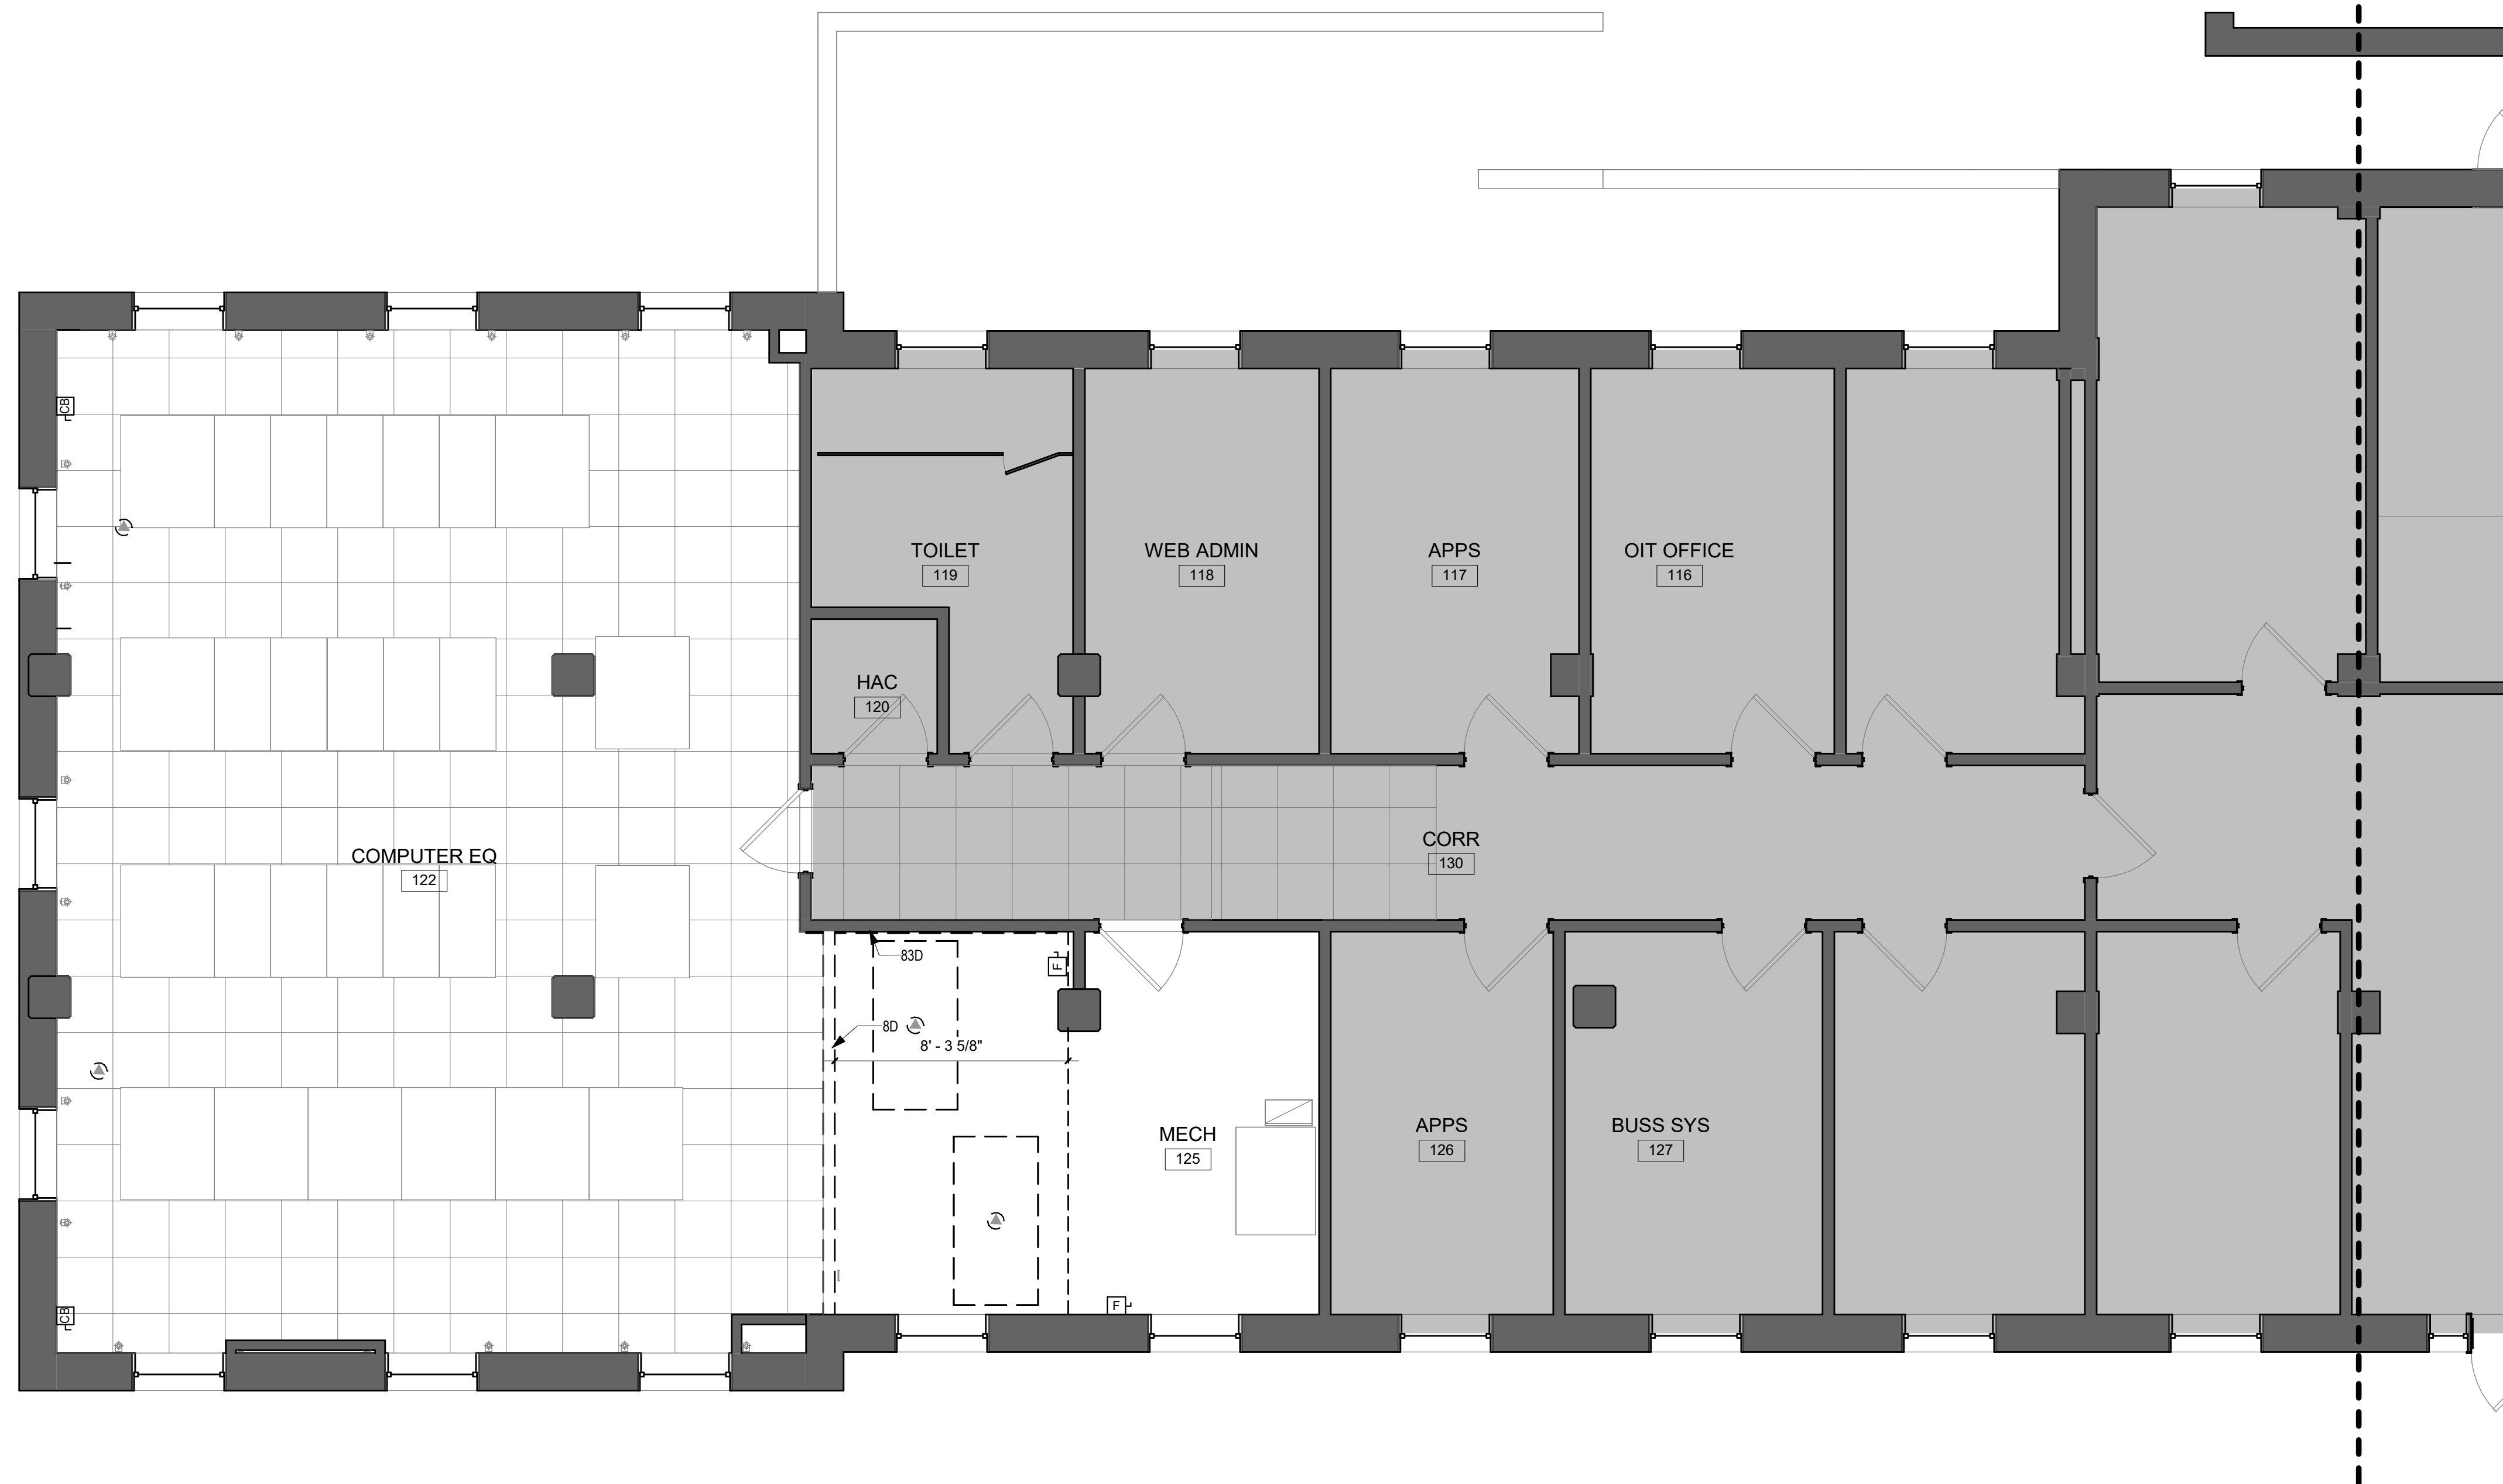

E4 PARTIAL DEMOLITION PLAN FIRST FLOOR 1/4" = 1'-0"



GENERAL NOTES DEMOLITION

- 1.GD FIELD VERIFY ALL EXISTING CONDITIONS, PRIOR TO START OF DEMOLITION. BRING SIGNIFICANT DISCREPANCIES TO THE ATTENTION OF THE C.O.R.
2.GD COORDINATE DEMOLITION PHASING AND SCHEDULE WITH THE C.O.R.
3.GD PROJECT EXISTING CONDITIONS AND DEMOLITION FROM DAMAGE DUE TO DEMOLITION, INCLUDING MECHANICAL & FIRE SUPPRESSION SYSTEMS.
4.GD SALVAGE AND RETURN TO OWNER EXISTING FIXTURES TO BE REMOVED PER DRAWINGS.
5.GD EXISTING WALL MOUNTED DEVICES TO REMAIN UNLESS NOTED OTHERWISE.
6.GD RELOCATE EXISTING WATER, DRAIN, CONDENSATE, & STEAM LINES OUTSIDE OF WALLS WHENEVER POSSIBLE. RELOCATE EXISTING LINES WHEN PASSING THROUGH TR WHERE UNABLE TO RELOCATE. REFER TO PLUMBING DRAWINGS FOR ADDITIONAL INFORMATION.
7.GD REFER TO MECHANICAL DRAWINGS FOR FAN, HILL, DIFFUSER, AND REGISTER DEMOLITION. CAP AND REPAIR AS REQUIRED.

GENERAL NOTES HAZARDOUS MATERIALS

- 1.3GH REMOVAL OF ASBESTOS CONTAINING AND OTHER POTENTIALLY HAZARDOUS MATERIALS FROM THE BUILDING MUST FOLLOW STATE AND FEDERAL REGULATIONS, AS WELL AS LOCAL LAWS WHEN APPLICABLE. REFER TO THE HAZMAT REPORT FOR A COMPLETE LIST OF ALL ASBESTOS-CONTAINING MATERIALS, SYSTEMS ROUTING AND PENETRATION LOCATIONS. CONTRACTOR SHALL DETERMINE MITIGATION QUANTITIES BASED ON THEIR SELECTED REMEDIATION LOCATION.
- 2.2GH CONTRACTOR MAY ROUTE CONDUIT PATHS TO AVOID POTENTIAL ASBESTOS CONTAINING MATERIAL PROVIDED PATHWAY DOES NOT INCREASE THE EXISTING LENGTH OF CONDUIT RUN.
- 3.3GH REFER TO ARCHITECTURAL, MECHANICAL, ELECTRICAL AND TELECOM DRAWINGS FOR SPECIFIC SCOPE OF DEMOLITION REQUIRED WORK. CONTRACTORS, BUT IS NOT NECESSARILY LIMITED TO, INCLUDING, BUT NOT LIMITED TO, EQUIPMENT, REFER TO HAZARDOUS MATERIALS SURVEYS FOR EXPECTED PRESENCE OF HAZARDOUS MATERIALS. ABATE AS REQUIRED.
- 4.4GH CONTRACTOR SHALL FOLLOW ALL APPLICABLE HAZMAT MATERIAL SAMPLING WITHIN THE PROJECT WORK LIMITS. THE CONTRACTOR MUST NOTIFY THE GOVERNMENT OF ANY ADDITIONAL MATERIALS REQUIRING ABATEMENT THAT ARE NOT IDENTIFIED IN THE HAZMAT REPORT PREPARED BY A/E.

REFERENCE KEYNOTES

- | | |
|-----|--|
| 8D | DEMOLISH EXISTING WALL. PROTECT AND SUPPORT TEMPORARILY EXISTING EQUIPMENT DURING DEMOLITION THEN REINSTALL PER NOTE 24R |
| 83D | REMOVE DRYWALL SHEATHING FROM INTERIOR FACE OF WALL ONLY. |

PARTITION GRAPHIC LEGEND

GRAPHIC	DESCRIPTION	PRIORITY
	NEW CONSTRUCTION	
	EXISTING PARTITION	
	TO BE DEMOLISHED	
	2 HR SMOKE / FIRE	1
	2 HR SHAFT	2
	2 HR FIRE	3
	1 HR SMOKE / FIRE	4
	1 HR FIRE	5
	HAZARDOUS	6
	NON RATED PARTITION	7

Revisions: 10% BASIS OF DESIGN 35% SCHEMATIC DESIGN 65% DESIGN DEVELOPMENT 95% CONSTRUCTION DOCUMENTS 95% CONSTRUCTION DOCUMENTS - REV 1 100% CONSTRUCTION DOCUMENTS	Date: 09/27/2023 10/27/2023 04/07/2025 06/12/2025 08/15/2025 10/20/2025	CONSULTANT CONSULTANT:	ARCHITECT/ENGINEER OF RECORD A/E: GDM-AE, Inc. 1308 NE 134th ST. SUITE A VANCOUVER, WA 98685 P: 541.436.4723 WWW.GDM-AE.COM ERIC SHREEVE	STAMP 	STATION 538	DRAWING TITLE PARTIAL FIRST FLOOR DEMOLITION PLAN	PHASE 100% CONSTRUCTION DOCUMENT	PROJECT TITLE VA CHILLICOTHE (EHRM) ELECTRONIC HEALTH RECORDS MODERNIZATION INFRASTRUCTURE UPGRADES	PROJECT NO. 538-21-705 BUILDING NO. 18
					VA U.S. Department of Veterans Affairs	APPROVED: RYAN JETER FOR OFFICIAL USE ONLY (FOUO) NOT FOR CONSTRUCTION	FLS FULLY SPRINKLERED	LOCATION 17273 STATE ROUTE 104 CHILLICOTHE, OH 45601-9715 ISSUE DATE 10/20/2025 CHECKED BY ES DRAWN BY GS	DRAWING NO. 018-AD-120



 GYP. BD. CEILING SYSTEM

 2 X 2 ACOUSTICAL LAY-IN CEILING SYSTEM.

 DOWN LIGHT FIXTURE

PROJECT NO.
538-21-705

BUILDING NO.
18


DRAWING NO.
018-AD-121




B4 EXISTING CONDITIONS



D4 EXISTING CONDITIONS

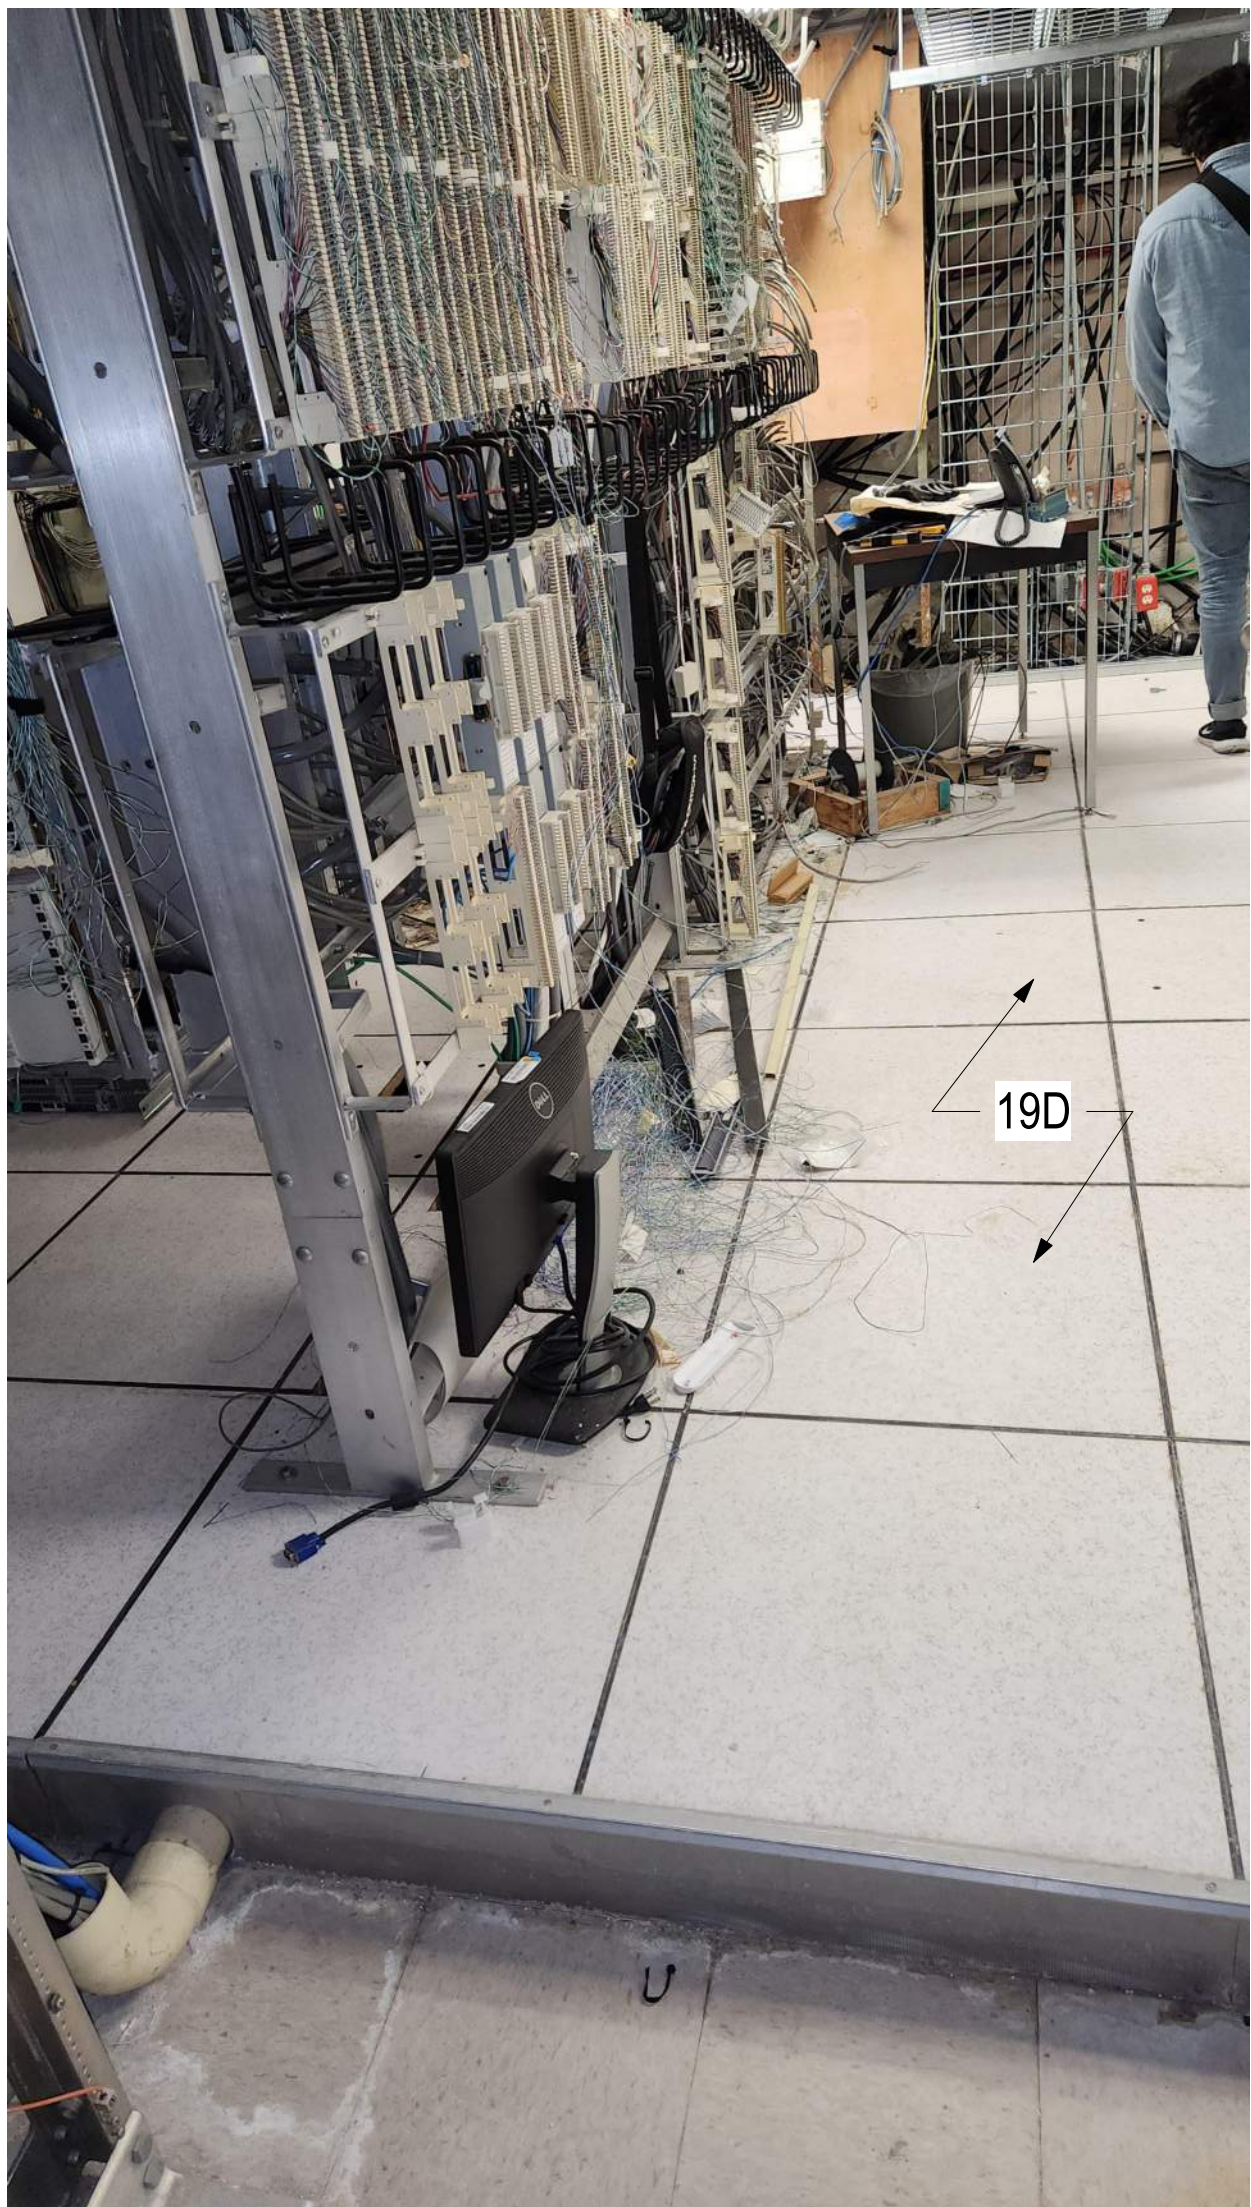

D9 EXISTING CONDITIONS

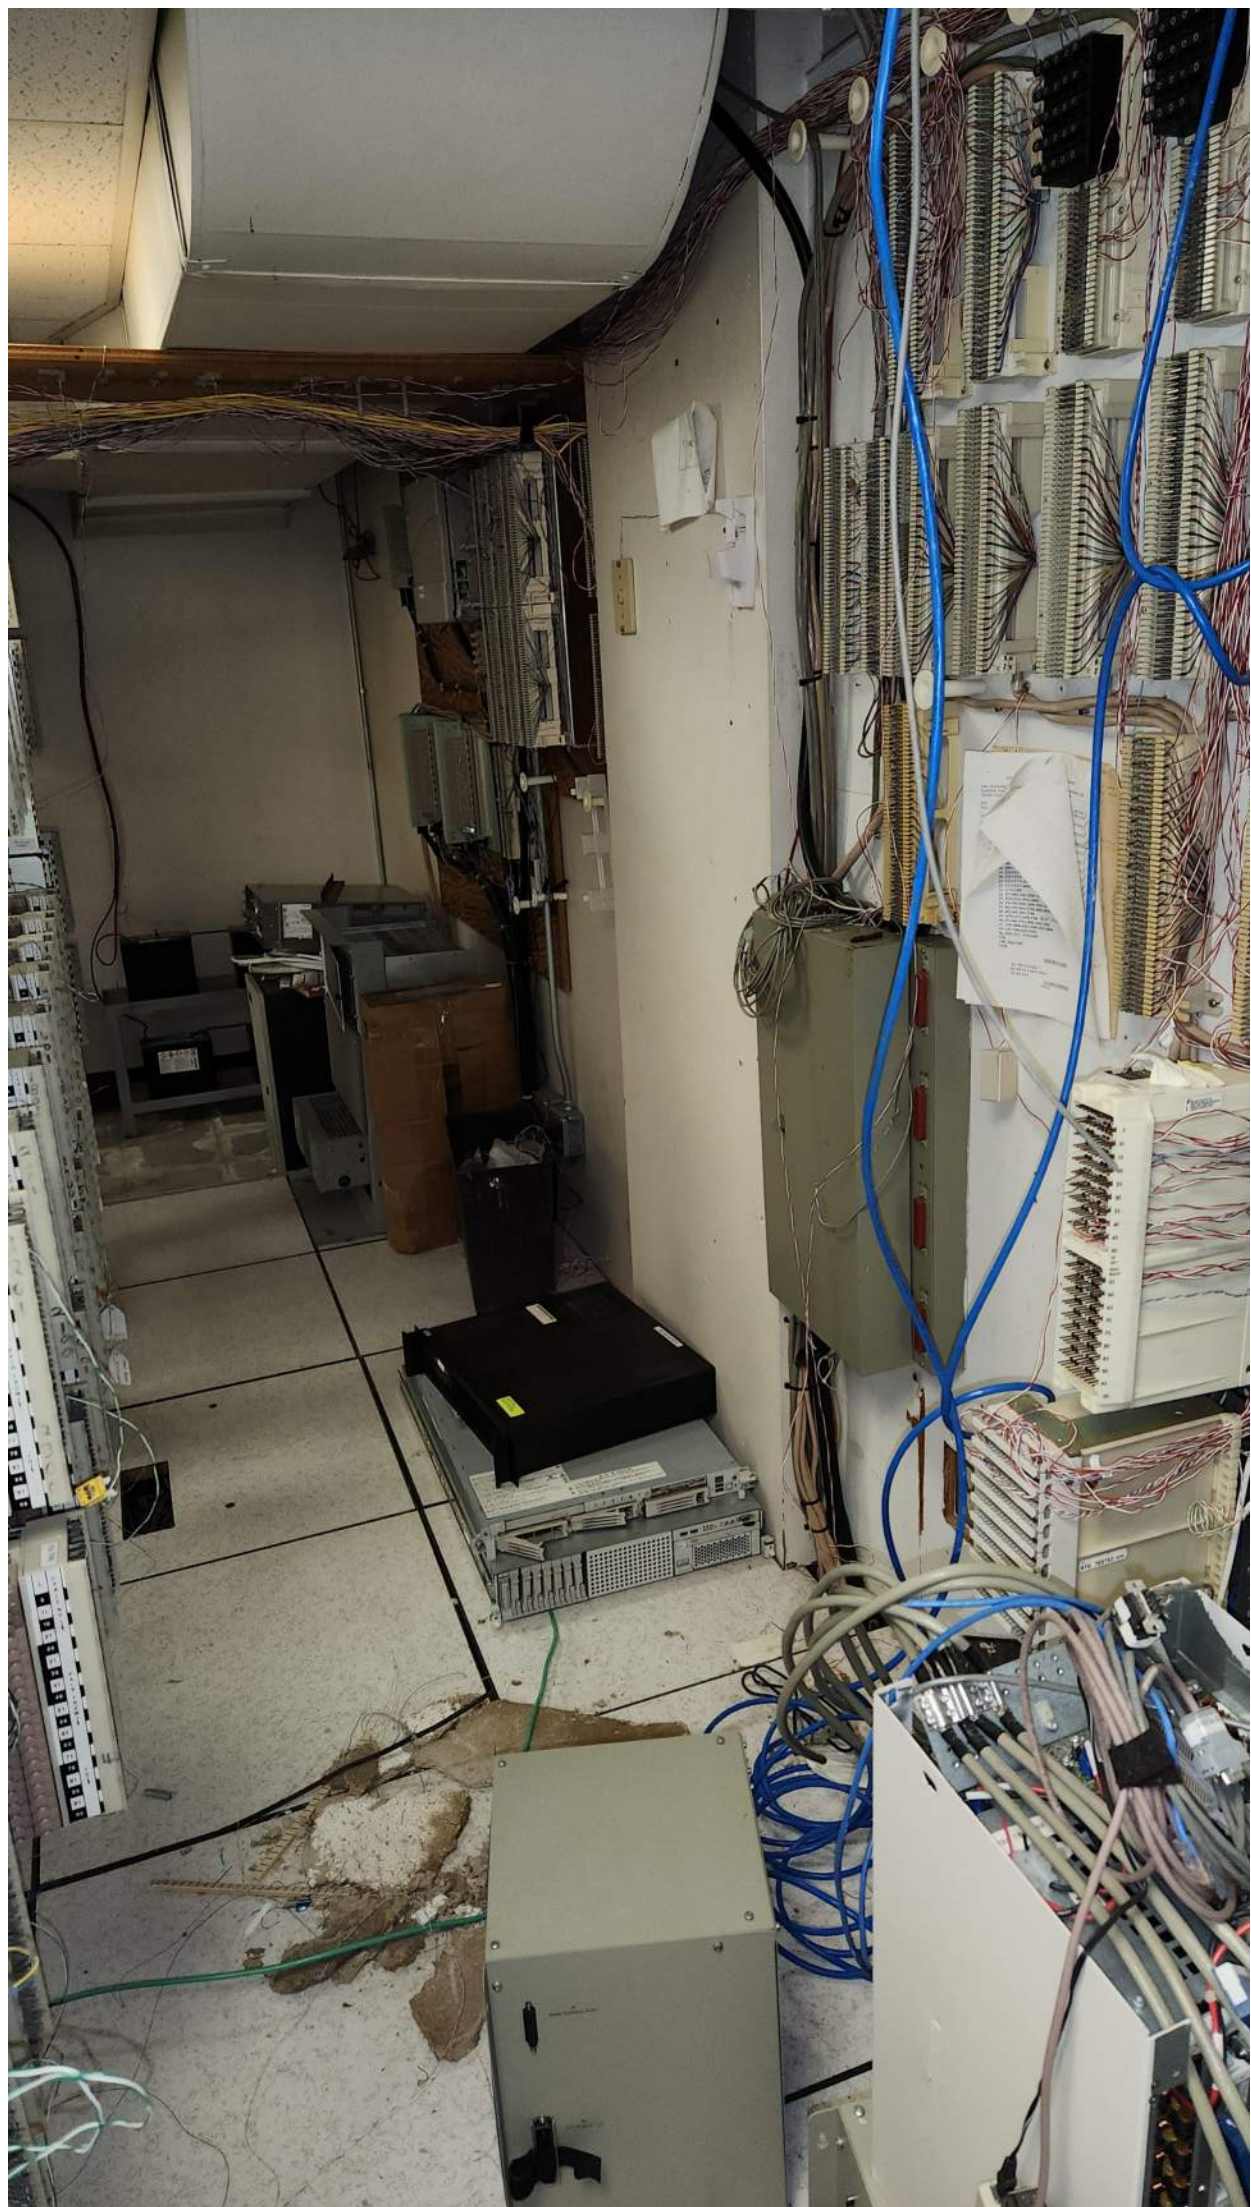

REFERENCE KEYNOTES

REFERENCE KEYNOTES	
19D	EXISTING RAISED FLOORING AND SUPPORTS TO REMAIN. PROTECT FROM DAMAGE AND CLEAN
66D	EXISTING ELECTRICAL EQUIPMENT TO REMAIN.
73D	EXISTING WALL MOUNTED EQUIPMENT TO BE RELOCATED TO ADJACENT WALL.



F7 EXISTING CONDITIONS