



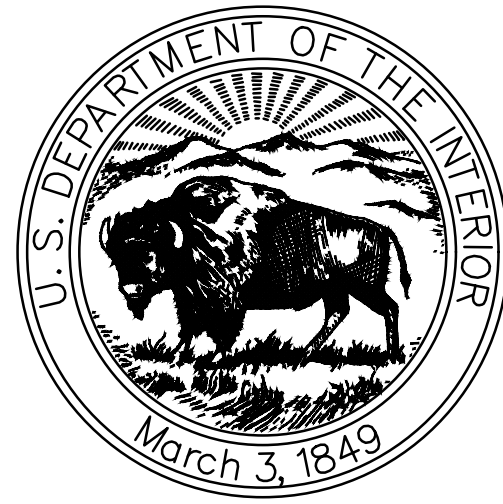


UNITED STATES DEPARTMENT OF THE INTERIOR
BUREAU OF LAND MANAGEMENT
BLM-NV ELY DISTRICT OFFICE

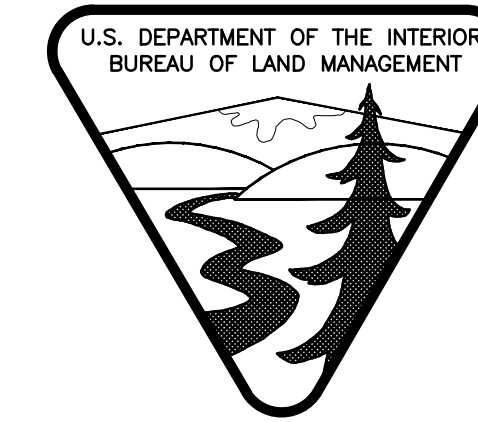


IDIQ CONTRACT NO. 140L0621D0006
GARNET HILL RECREATION AREA


100% CONSTRUCTION DOCUMENTS

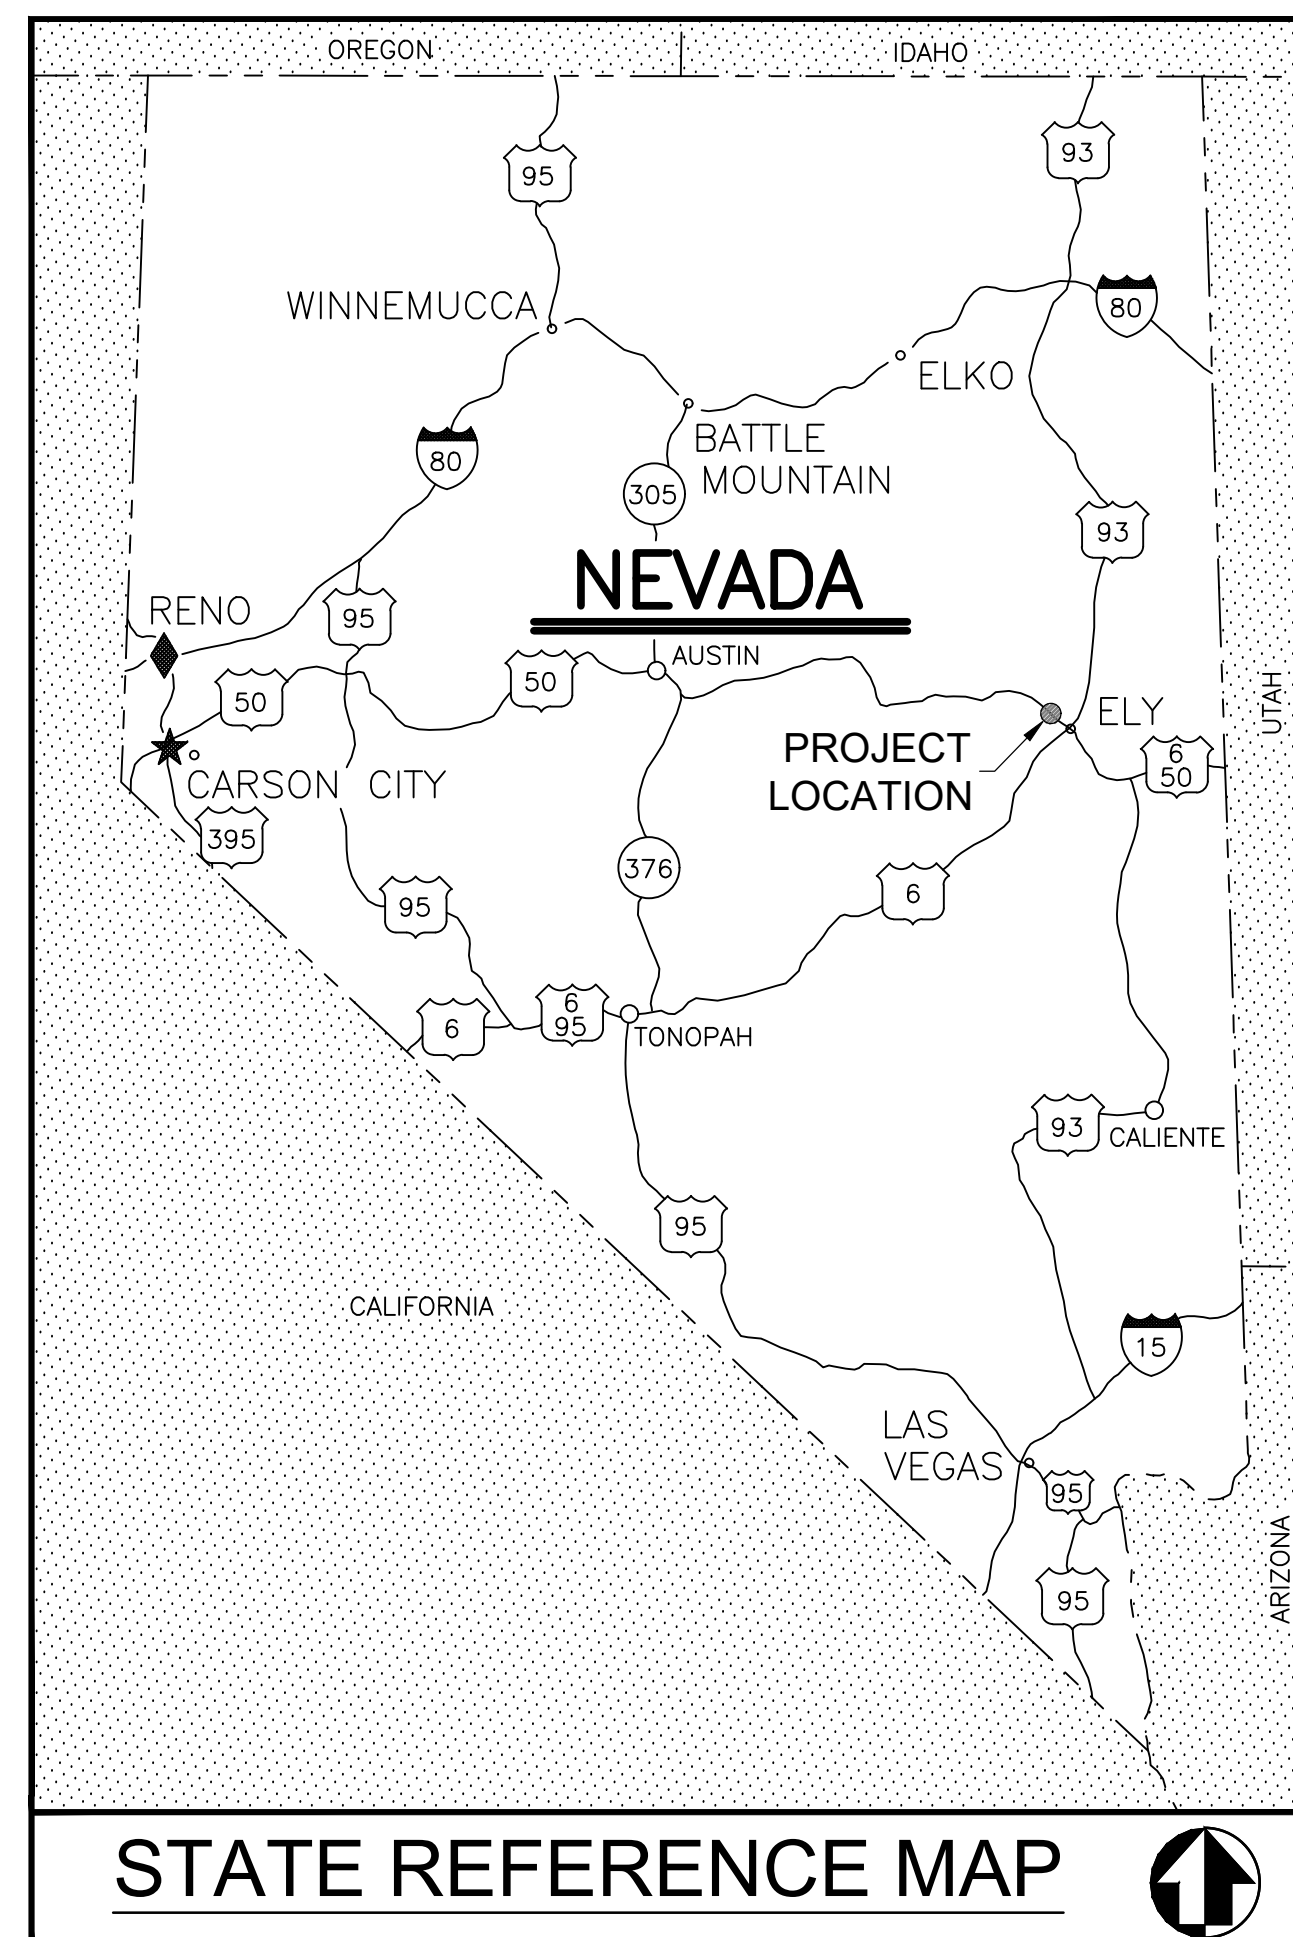

STATE REFERENCE MAP

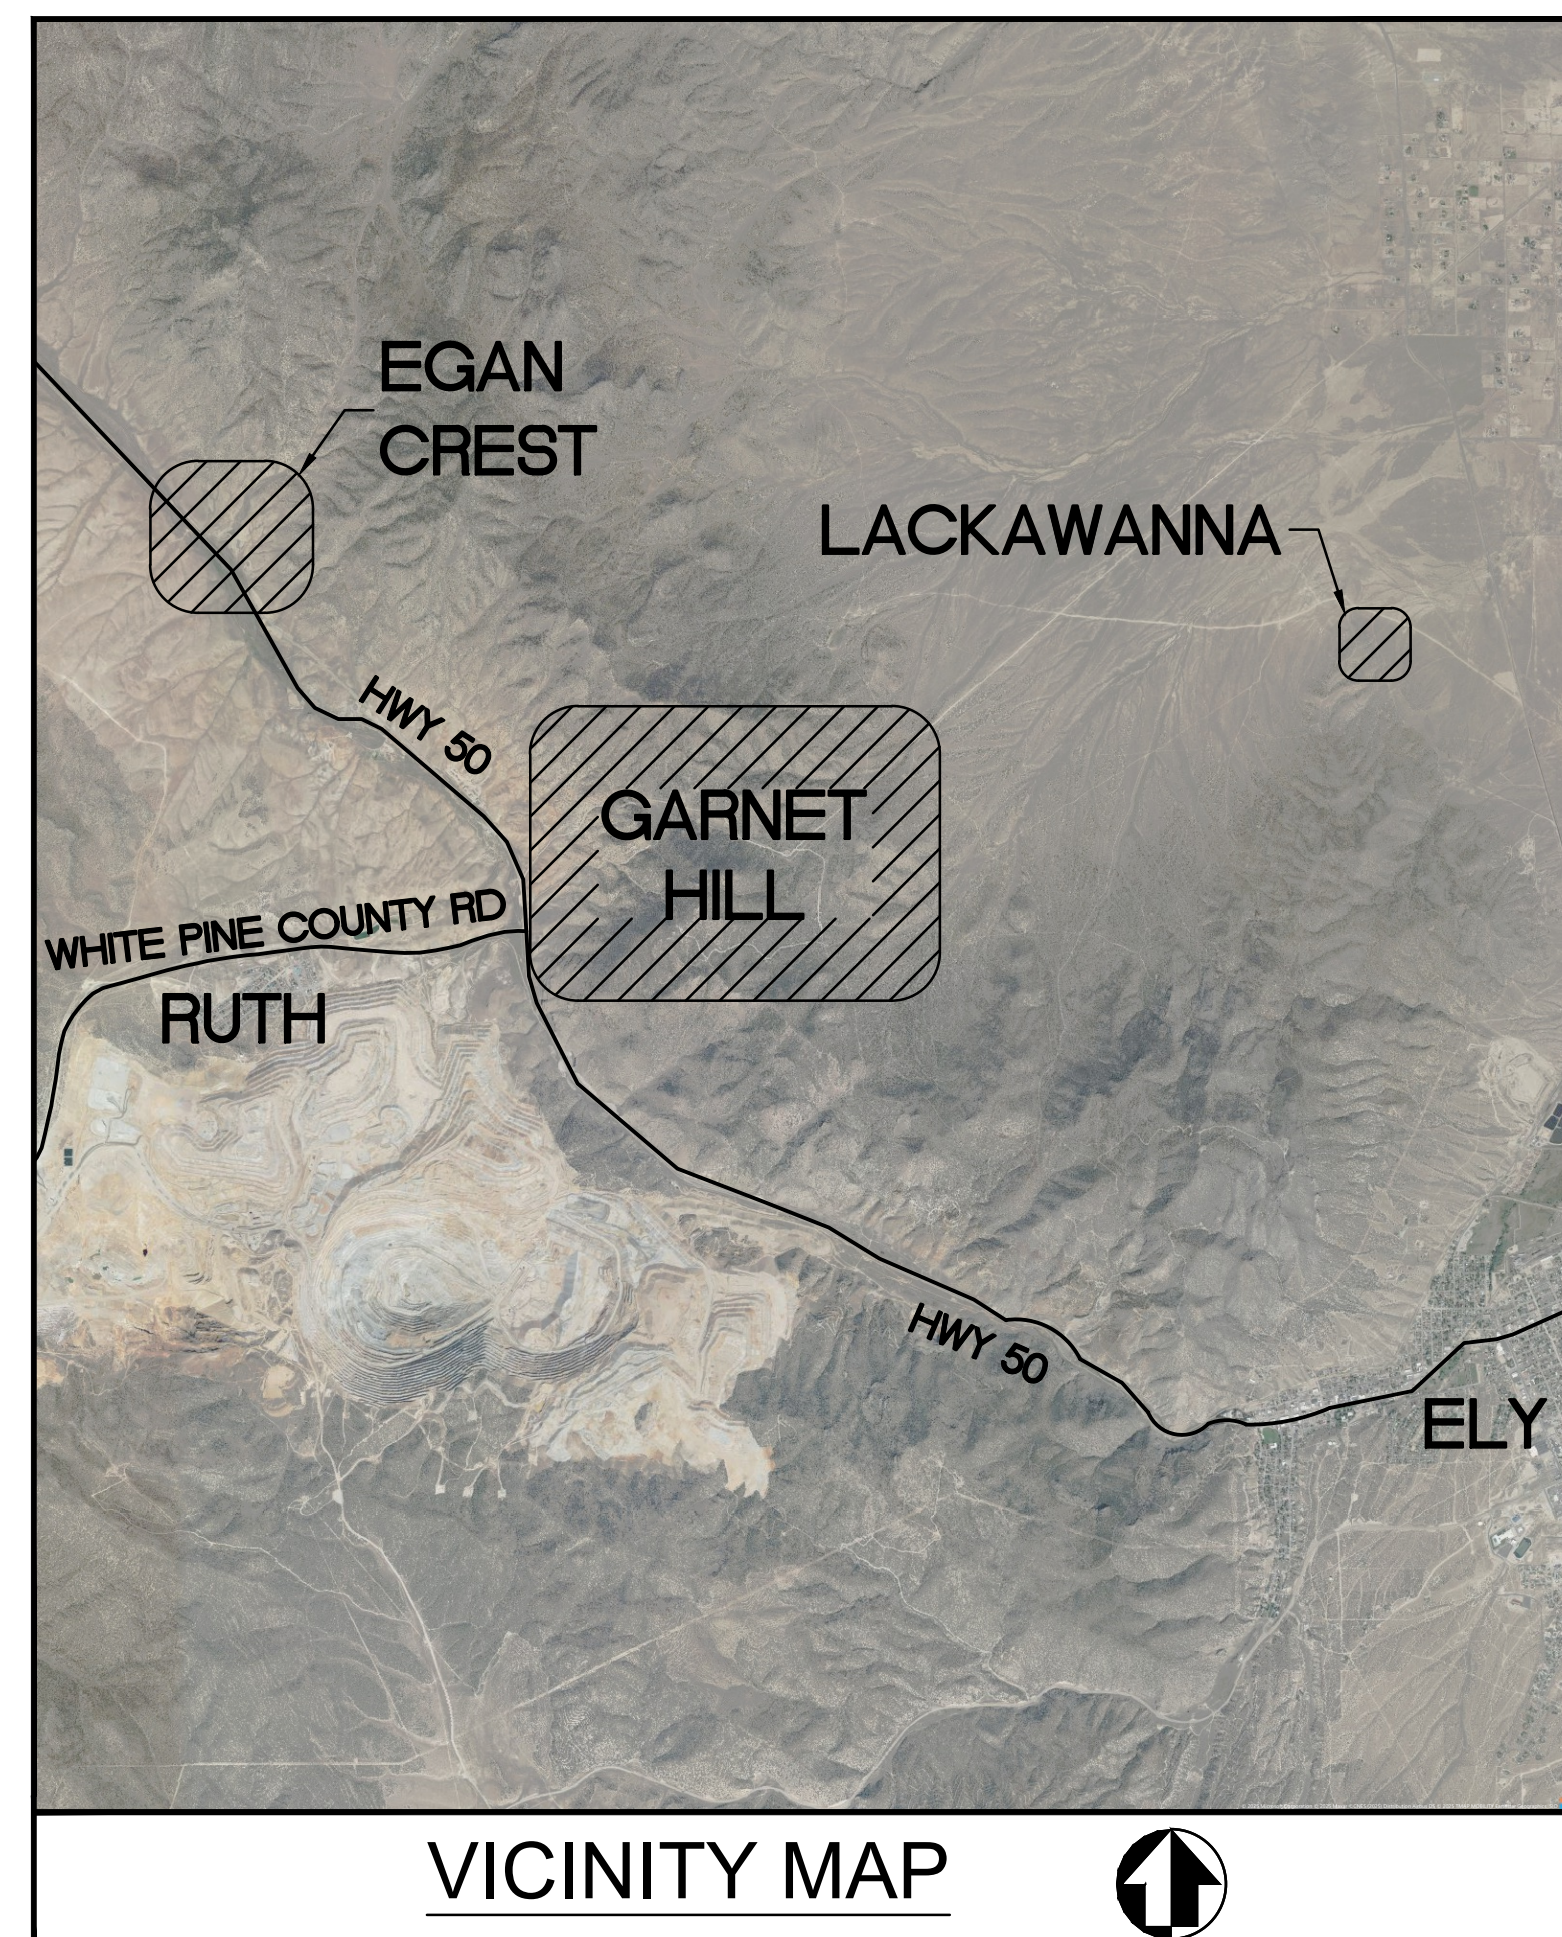

VICINITY MAP

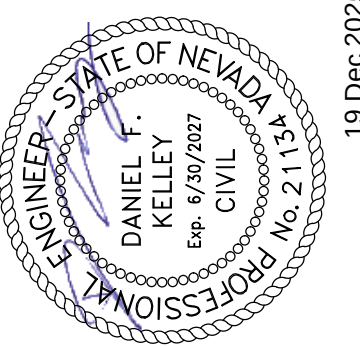

19 Dec 2025

UNITED STATES DEPARTMENT OF THE INTERIOR
BUREAU OF LAND MANAGEMENT
**GARNET HILL RECREATION AREA
TITLE I AND II SERVICES**
BUREAU OF LAND MANAGEMENT DISTRICT OFFICE
ELY, NEVADA

Revision Issue	Issue Date
Rev. #	12/16/2025
Description	100% CONSTRUCTION DOCUMENTS
Project Status	BLM Project # 140L0621D0006
Drawn By	A. BROWN
Checked By	D. KELLEY

GENERAL SHEETS
COVER SHEET

G-001

P:\Projects\BLM - NV & CA ID\Task Orders\Task 27 - Garnet Hill Recreation Area Title 1 & II Services\Engineering\Drawings\Production Drawings\00 - COVER & OVERALL\208-003-G.dwg, 12/16/2025 8:16 AM ABBROWN

CIVIL ABBREVIATIONS

A, AMPS	AMPERES	HWR	HOT WATER RETURN
AB	ANCHOR BOLT	HWS	HOT WATER SUPPLY
ABBR	ABBREVIATION		
AC	ASPHALT CONCRETE	ID	INSIDE DIAMETER
ACP	ASBESTOS CEMENT PIPE	IN	INCH
ADMIN	ADMINISTRATION	INSUL	INSULATION
AGGR	AGGREGATE	INVT	INVERT
AIP	ABANDONED IN PLACE		
AL	ALUMINUM	JT	JOINT
ALT	ALTERNATE		
ANSI	AMERICAN NATIONAL STANDARDS INSTITUTE	LBS	POUNDS
APVD	APPROVED	LG	LENGTH, LONG
APPROX	APPROXIMATE	LP	LOW POINT
ASCE	AMERICAN SOCIETY OF CIVIL ENGINEERS	LT	LEFT
ASPH	ASPHALT	LTG	LIGHTING
ASTM	AMERICAN SOCIETY FOR TESTING AND MATERIALS		
		MAG	MAGNETIC
AWG	AMERICAN WIRE GAUGE	MAINT	MAINTENANCE
AUTO	AUTOMATIC	MATL	MATERIAL
AUX	AUXILIARY	MAX	MAXIMUM
AVG	AVERAGE	MECH	MECHANICAL
A/C	AIR CONDITIONING	MET	METAL
A/E	ARCHITECT/ENGINEER	MFR	MANUFACTURER
		MGD	MILLIONS GALLONS PER DAY
BFG	BELOW FINISH GRADE	MH	MANHOLE
BITUM	BITUMINOUS	MIN	MINIMUM
BLDG	BUILDING	MISC	MISCELLANEOUS
C, COMM	COMMUNICATIONS	N	NORTH
CAT	CATALOG	NIC	NOT IN CONTRACT
CEM	CEMENT	NIM	NON-INSULATED METAL
CI	CAST IRON	NOM	NOMINAL
CIP	CAST IRON PIPE	NORM	NORMAL
CHWR	CHILLED WATER RETURN	NTS	NOT TO SCALE
CHWS	CHILLED WATER SUPPLY	NV	NEVADA
CIRC	CIRCULAR	#, NO.	NUMBER
CKT BRK	CIRCUIT BREAKER		
CL	CENTER LINE	O/	OVER
CLG	CEILING	OC	ON CENTER
CLJ	CONTROL JOINT	OD	OUTSIDE DIAMETER
CLR	CLEAR, CLEARANCE	OHP	OVERHEAD POWER
CLVT	CULVERT	OPP	OPPOSITE
CMP	CORRUGATED METAL PIPE	OVHD	OVER HEAD
CMU	CONCRETE MASONRY UNITS	OSHA	OCCUPATIONAL SAFETY AND HEALTH ADMINISTRATION
CO	CONTRACTING OFFICER		
CONC	CONCRETE	P	POLE, POWER
CONDS	CONDUIT (S)	PE	PROJECT ENGINEER
CONN	CONNECTION	PIV	POST INDICATOR VALVE
CONSTR	CONSTRUCTION	PL	PLATE
COR	CONTRACTING OFFICER'S REPRESENTATIVE	PLCS	PLACES
CORP	CORPORATION	POC	POINT OF CONNECTION
CTR	CENTER	PT	POINT
CU	COPPER	PVC	POLYVINYL CHLORIDE
CW	CHILLED / COLD WATER	PVMT	PAVEMENT
CY	CUBIC YARD		
		RAD, R	RADIUS
DBL	DOUBLE	RD	ROAD
DEG	DEGREE	REF	REFERENCE
DET	DETAIL	REINF	REINFORCING
DI	DROP INLET	REQ'D	REQUIRED
DIA, Ø	DIAMETER	REVR	REVERSE
DIAG	DIAGONAL	REV	REVISIONS
DIM	DIMENSION	RM	ROOM
DIST	DISTANCE	RND	ROUND
DWG	DRAWING	RT	RIGHT
		RS	RIGID STEEL
E	EAST	S	SLOPE / SOUTH
EA	EACH	SCH, SHCED	SCHEDULE
EG	EXISTING GRADE	SCO	SEWER CLEANOUT
ELEC	ELECTRIC, ELECTRICAL	SDWK	SIDEWALK
ELEV	ELEVATION	SECT	SECTION
EMER	EMERGENCY	SH MET	SHEET METAL
ENCL	ENCLOSURE	SHLDR	SHOULDER
ENGR	ENGINEER	SHT	SHEET
ENTR	ENTRANCE	SIM	SIMILAR
EOP	EDGE OF PAVEMENT	SMH	SANITARY SEWER MANHOLE
EQL	EQUAL	SOW	STATEMENT OF WORK
EQUIP	EQUIPMENT	SPEC	SPECIFICATION
EX	EXISTING	SQ	SQUARE
EXP JT	EXPANSION JOINT	SS	SANITARY SEWER
EXP	EXPOSED	ST	STEAM
EXT	EXTERIOR	STA	STATION
		STD	STANDARD
		STL	STEEL
F	FIRE	TB	THRUST BLOCK
FF	FINISH FLOOR	TC	TOP OF CURB
FG	FINISH GRADE	TEL	TELEPHONE
FH	FIRE HYDRANT	THK	THICK
FTG	FITTING	TYP	TYPICAL
FL	FLOW LINE		
FO	FIBER OPTICS	UBC	UNIFORM BUILDING CODE
FP	FIRE PROTECTION	UGND	UNDERGROUND
FT	FOOT	UNFIN	UNFINISHED
FUT	FUTURE	US	UNITED STATES
GA	GAGE OR GAUGE	V	VOLTAGE
GALV	GALVANIZEDGPH		
GEN	GENERAL	W	WASTE, WATER, WEST, WIDTH
GFI	GROUND FAULT INTERRUPTER	WA	WASHINGTON
GND	GROUND	WSDOT	WASHINGTON STATE DEPARTMENT OF TRANSPORTATION
GOVT	GOVERNMENT	WT	WEIGHT
GPH	GALLONS/HOUR	WTR	WATER
GPM	GALLONS/MINUTE		
GR	GRADE	XFMR	TRANSFORMER
GV	GATE VALVE		
GW	GUY-WIRE	YD	YARD
GYP	GYPSUM		
H	HOUR		
HAZ W	HAZARDOUS WASTE		
HPT	HIGH POINT		
HORIZ	HORIZONTAL		
HT	HEIGHT		
HW	HOT WATER		


SYMBOLS LEGEND

		EXISTING	PROPOSED	
	DETAIL NUMBER			CONCRETE SIDEWALK
	REFERENCE DRAWING NUMBER			ASPHALT
	SECTION NUMBER			GRAVEL
	REFERENCE DRAWING NUMBER			VEGETATION
	DIMENSION			ELECTRICAL CONDUIT
	KEYNOTE INDICATOR - DEMO			COMMUNICATIONS CONDUIT
	KEYNOTE INDICATOR - CONSTRUCTION			WATER LINE
	KEYNOTE INDICATOR - DETAIL PART			FIRE WATER LATERAL
	KEY NOTE SYMBOL			SANITARY SEWER PIPE
	MATCHLINE			STORM DRAIN PIPE
	NORTH ARROW FOR 22"x34" PLANS			SANITARY SEWER MANHOLE
	NORTH ARROW FOR VICINITY MAPS			SANITARY SEWER CLEANOUT
	GRAPHIC (BAR) SCALE			FIRE HYDRANT
	REVISION INDICATOR (SHOWN WITH CLOUD)			WATER VALVE
	EXISTING MAJOR CONTOUR			ELECTRICAL PULL BOX
	EXISTING MINOR CONTOUR			COMMUNICATIONS HAND HOLE
	PROPOSED MAJOR CONTOUR			ANTI-RAM PREVENTION BOULDER
	PROPOSED MINOR CONTOUR			BOLLARD
				COMM MANHOLE

Sheet List Table

Sheet Number	Sheet Title
G-001	COVER SHEET
G-002	LEGEND AND ABBREVIATION
V-001	TOPOGRAPHIC SURVEY CONTROL EXHIBIT
V-002	TOPOGRAPHIC SURVEY CONTROL EXHIBIT
C-100	OVERALL
1CS101	LACKAWANNA SITE PLAN
1CG101	LACKAWANNA GRADING PLAN
2CR101	EGAN CREST DEMOLITION PLAN
2CS101	EGAN CREST SITE PLAN
2CG101	EGAN CREST GRADING PLAN
3CR101	KEYSTONE DEMOLITION PLAN
3CS-101	KEYSTONE SITE PLAN
3CG101	KEYSTONE GRADING PLAN
4CR101	LOWER CAMPGROUND DEMOLITION PLAN
4CS101	LOWER CAMPGROUND SITE PLAN
4CG101	LOWER CAMPGROUND GRADING PLAN
4CG102	LOWER CAMPGROUND GRADING PLAN
5CR101	UPPER CAMPGROUND DEMOLITION PLAN
5CS101	UPPER CAMPGROUND SITE PLAN
5CG101	UPPER CAMPGROUND GRADING PLAN
5CG102	UPPER CAMPGROUND GRADING PLAN
6CR101	MAIN TRAIL DEMOLITION PLAN
6CS101	MAIN TRAIL SITE PLAN
6CG101	MAIN TRAIL GRADING PLAN 1
6CG102	MAIN TRAIL GRADING PLAN 2

Sheet Number	Sheet Title
6CG103	MAIN TRAIL GRADING SECTIONS
7CP101	POLE LINE ROAD PLAN & PROFILE
7CP102	POLE LINE ROAD PLAN & PROFILE
7CP103	POLE LINE ROAD PLAN & PROFILE
7CP104	POLE LINE ROAD PLAN & PROFILE
7CP105	POLE LINE ROAD PLAN & PROFILE
7CP106	POLE LINE ROAD PLAN & PROFILE
7CP107	POLE LINE ROAD PLAN & PROFILE
7CP108	POLE LINE ROAD PLAN & PROFILE
7CP109	POLE LINE ROAD PLAN & PROFILE
7CP110	POLE LINE ROAD PLAN & PROFILE
7CP111	POLE LINE ROAD PLAN & PROFILE
7CP112	POLE LINE ROAD PLAN & PROFILE
7CP113	POLE LINE ROAD PLAN & PROFILE
7CP114	POLE LINE ROAD PLAN & PROFILE
7CP115	POLE LINE ROAD PLAN & PROFILE
7CP116	POLE LINE ROAD PLAN & PROFILE
7CP117	POLE LINE ROAD PLAN & PROFILE
7CP118	POLE LINE ROAD PLAN & PROFILE
7CP501	TYPICAL SECTIONS
CD501	CIVIL DETAILS 1
CD502	CIVIL DETAILS 2
CD503	CIVIL DETAILS 3
CD504	CIVIL DETAILS 4
CD505	CIVIL DETAILS 5

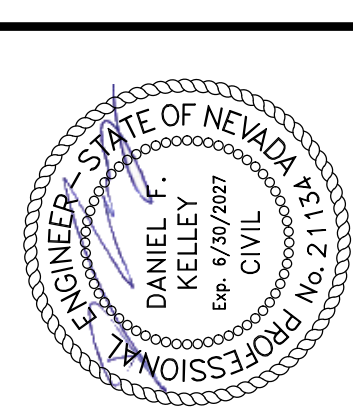

GARNET HILL RECREATION AREA TITLE I AND II SERVICES

UNITED STATES DEPARTMENT OF THE INTERIOR
BUREAU OF LAND MANAGEMENT

BUREAU OF LAND MANAGEMENT DISTRICT OFFICE
ELY, NEVADA

Project Status	Issue Date
100% CONSTRUCTION DOCUMENTS	12/16/2025
BLM Project #	140L0621D0006
Drawn By	ABBROWN
Checked By	D.KELLEY


Revision Issue	Date
Description	
Rev. #	

GENERAL SHEETS
LEGEND AND ABBREVIATION


G-002



P:\Projects\BLM - NV & CA\IDOTask Orders\Task 27 - Garnet Hill Recreation Area Title I & II Services\Engineering\Drawings\Production Drawings\00 - COVER & OVERALL\1208-005-CO.dwg 12/16/2025 8:13 AM KMALVESTUTO

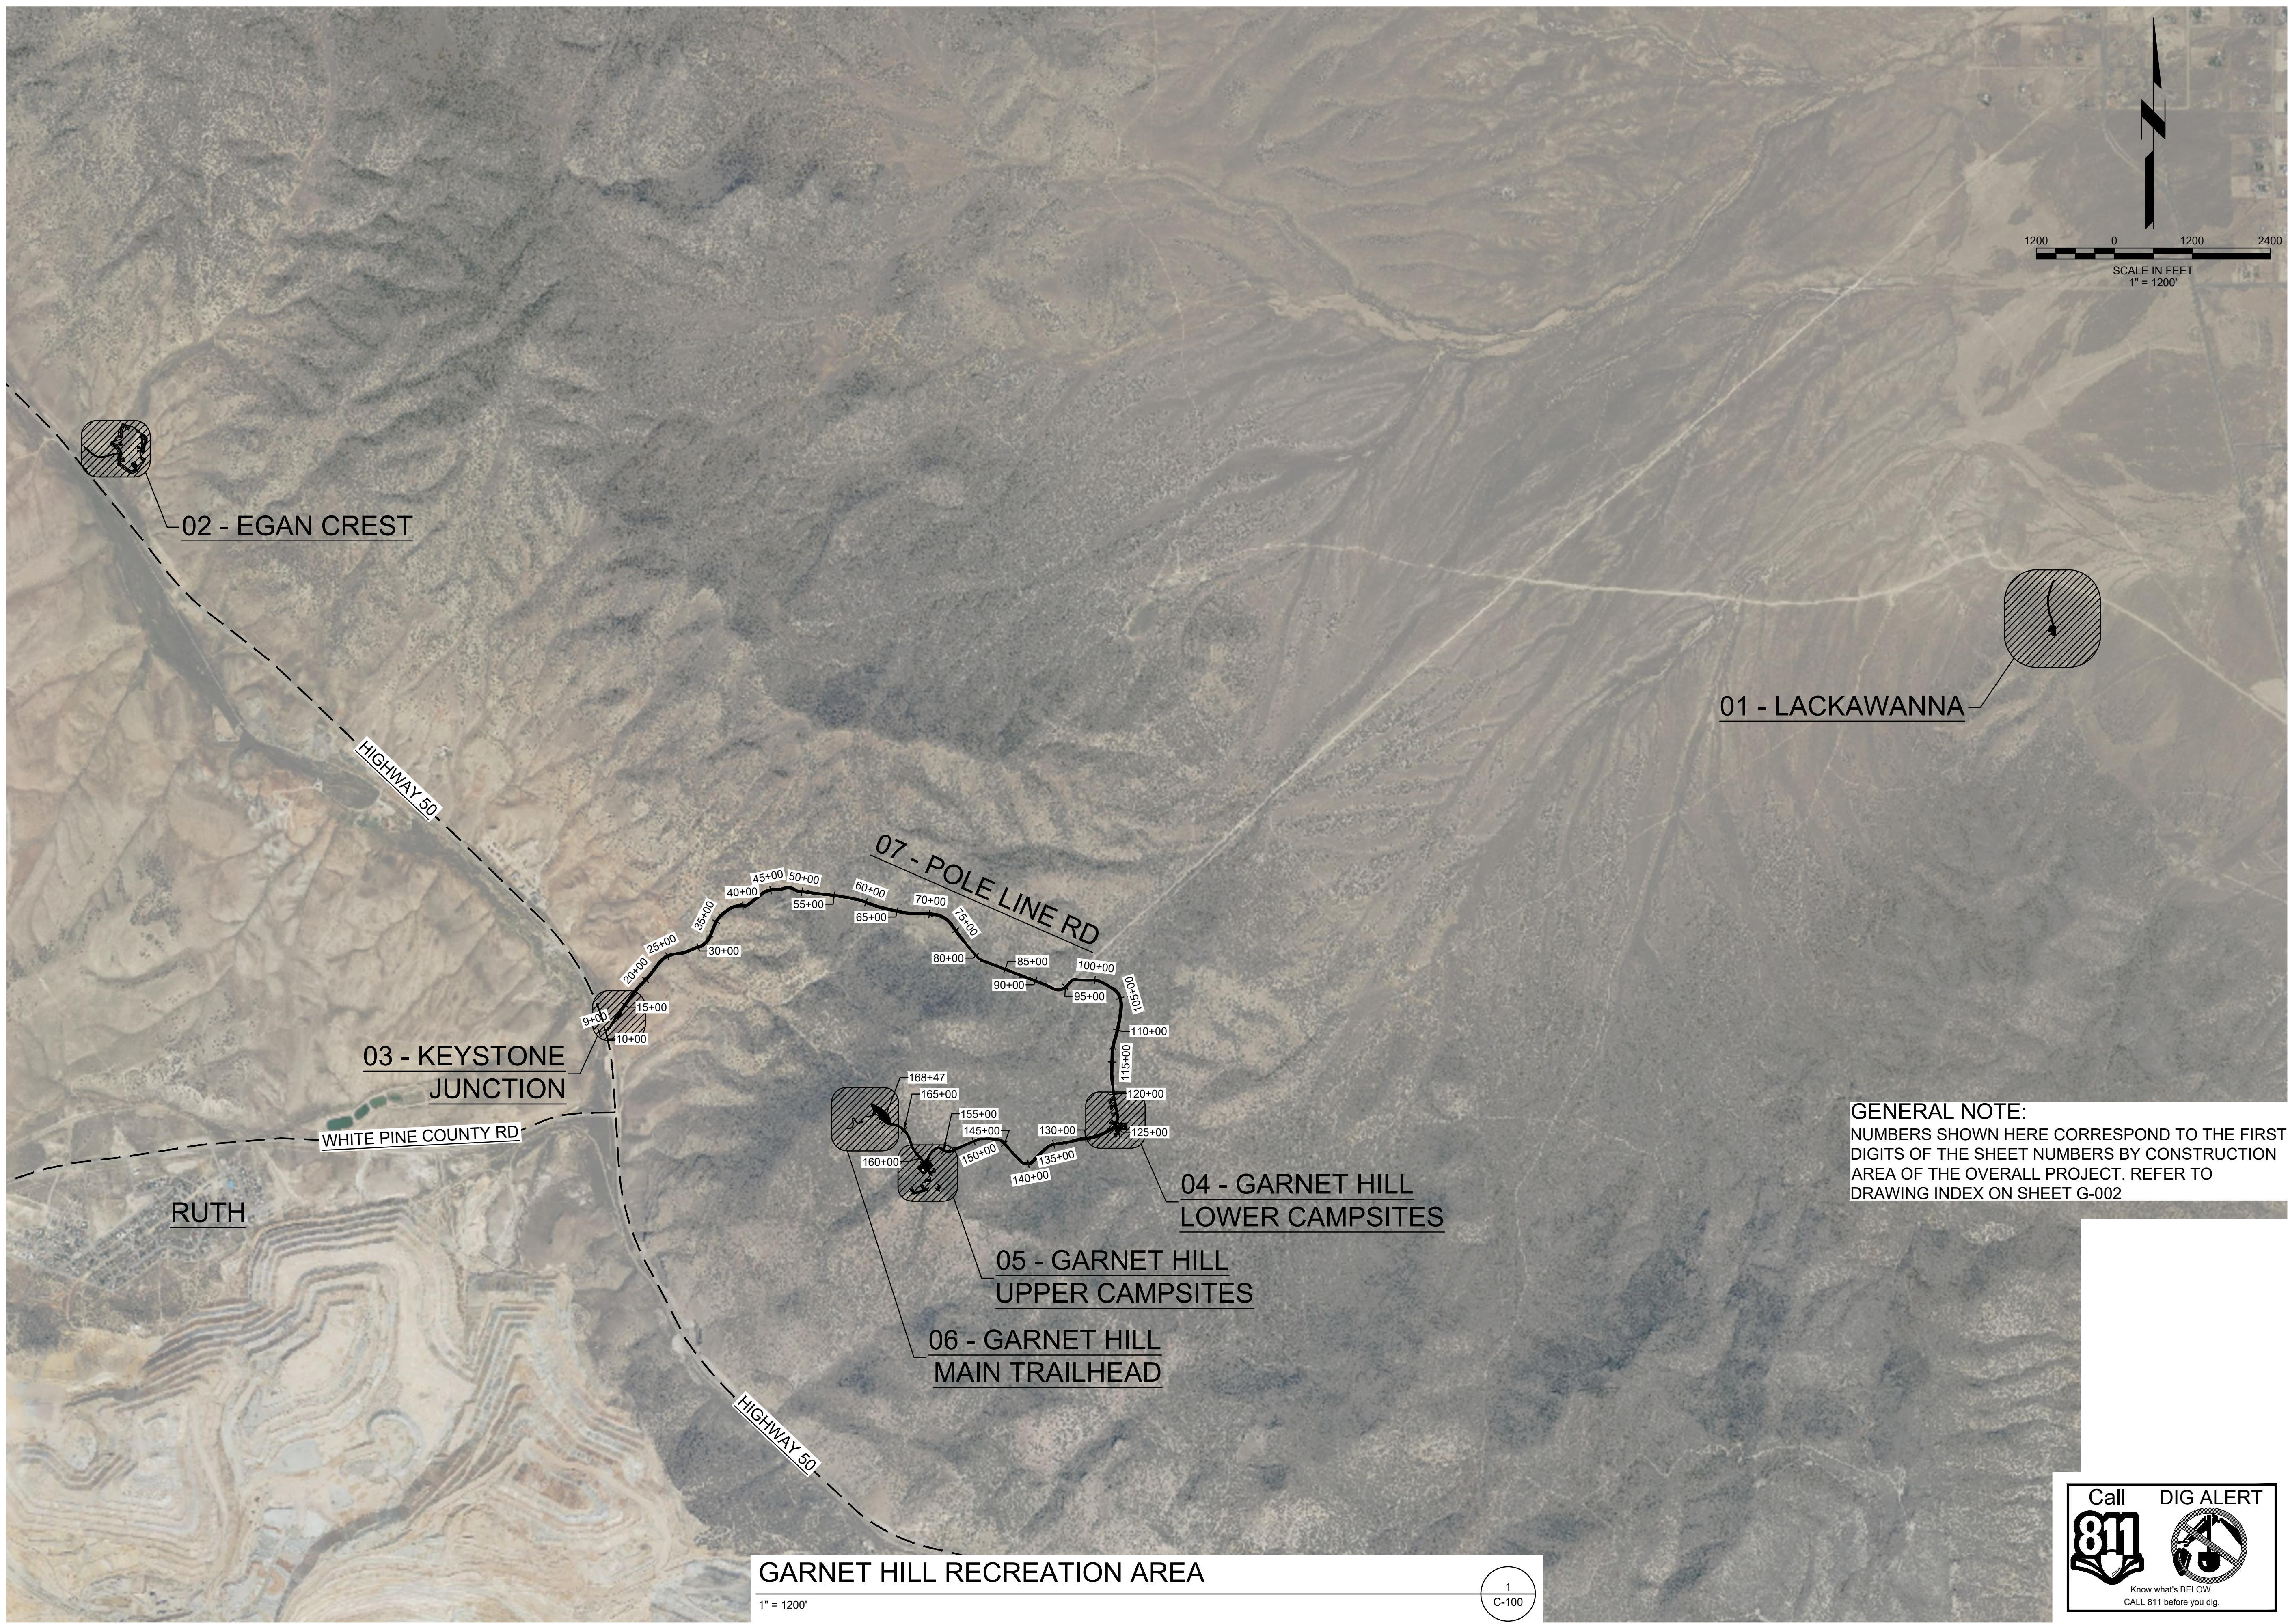

GENERAL NOTE:
NUMBERS SHOWN HERE CORRESPOND TO THE FIRST DIGITS OF THE SHEET NUMBERS BY CONSTRUCTION AREA OF THE OVERALL PROJECT. REFER TO DRAWING INDEX ON SHEET G-002

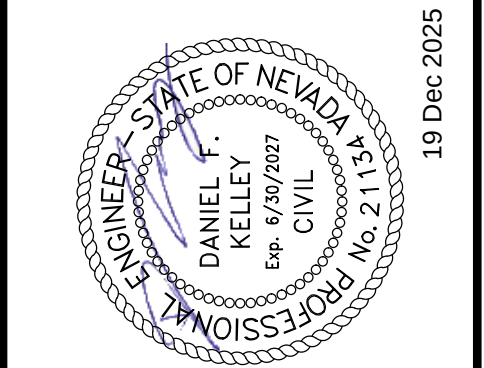


UNITED STATES DEPARTMENT OF THE INTERIOR
BUREAU OF LAND MANAGEMENT
**GARNET HILL RECREATION AREA TITLE I
AND II SERVICES**
BUREAU OF LAND MANAGEMENT DISTRICT OFFICE
ELY, NEVADA

Project Status	Issue Date
100% CONSTRUCTION DOCUMENTS	12/16/2025
BLM Project #	
140L0621D0006	A. BROWN D. KELLEY
Drawn By	
Checked By	

Revision Issue	Date
Description	Rev. #



GENERAL SHEETS
OVERALL
C-100

P:\Projects\BLM - NV & CA IDIO\Task Orders\Task 27 - Garnet Hill Recreation Area Title I & II Services\Engineering\Drawings\Production Drawings\01 - LACKAWANNA\2018-003-01-CS.dwg 12/16/2025 8:13 AM KVAL VESTUITO

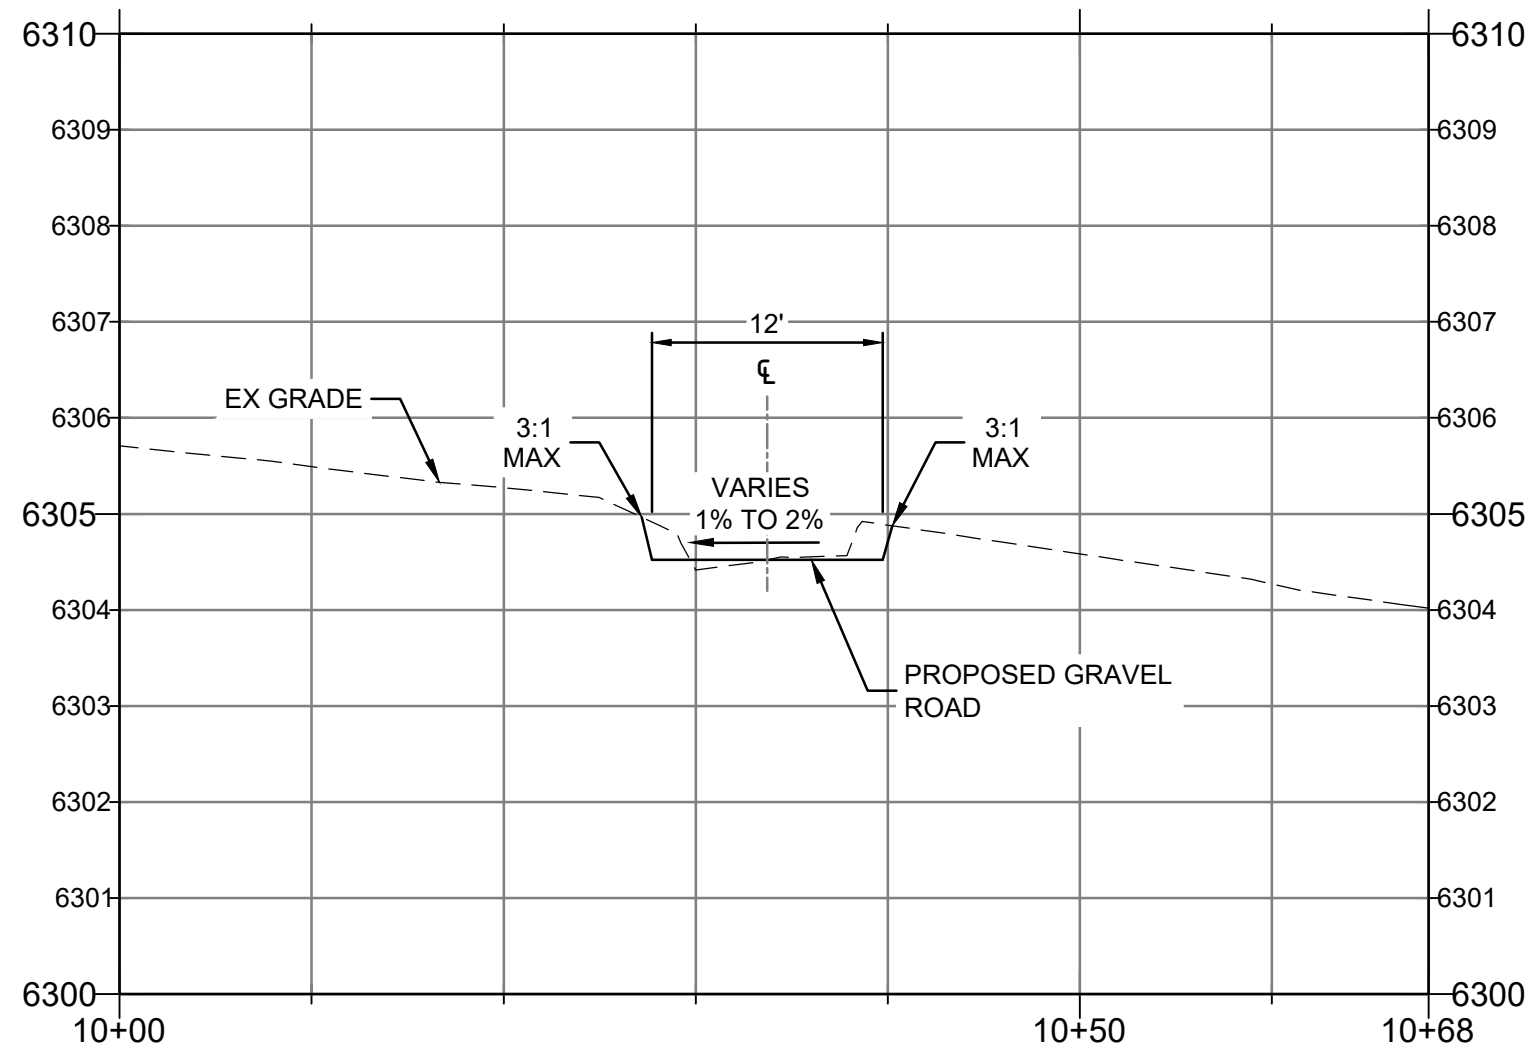



TYPICAL ROAD SECTION

1" = 10'

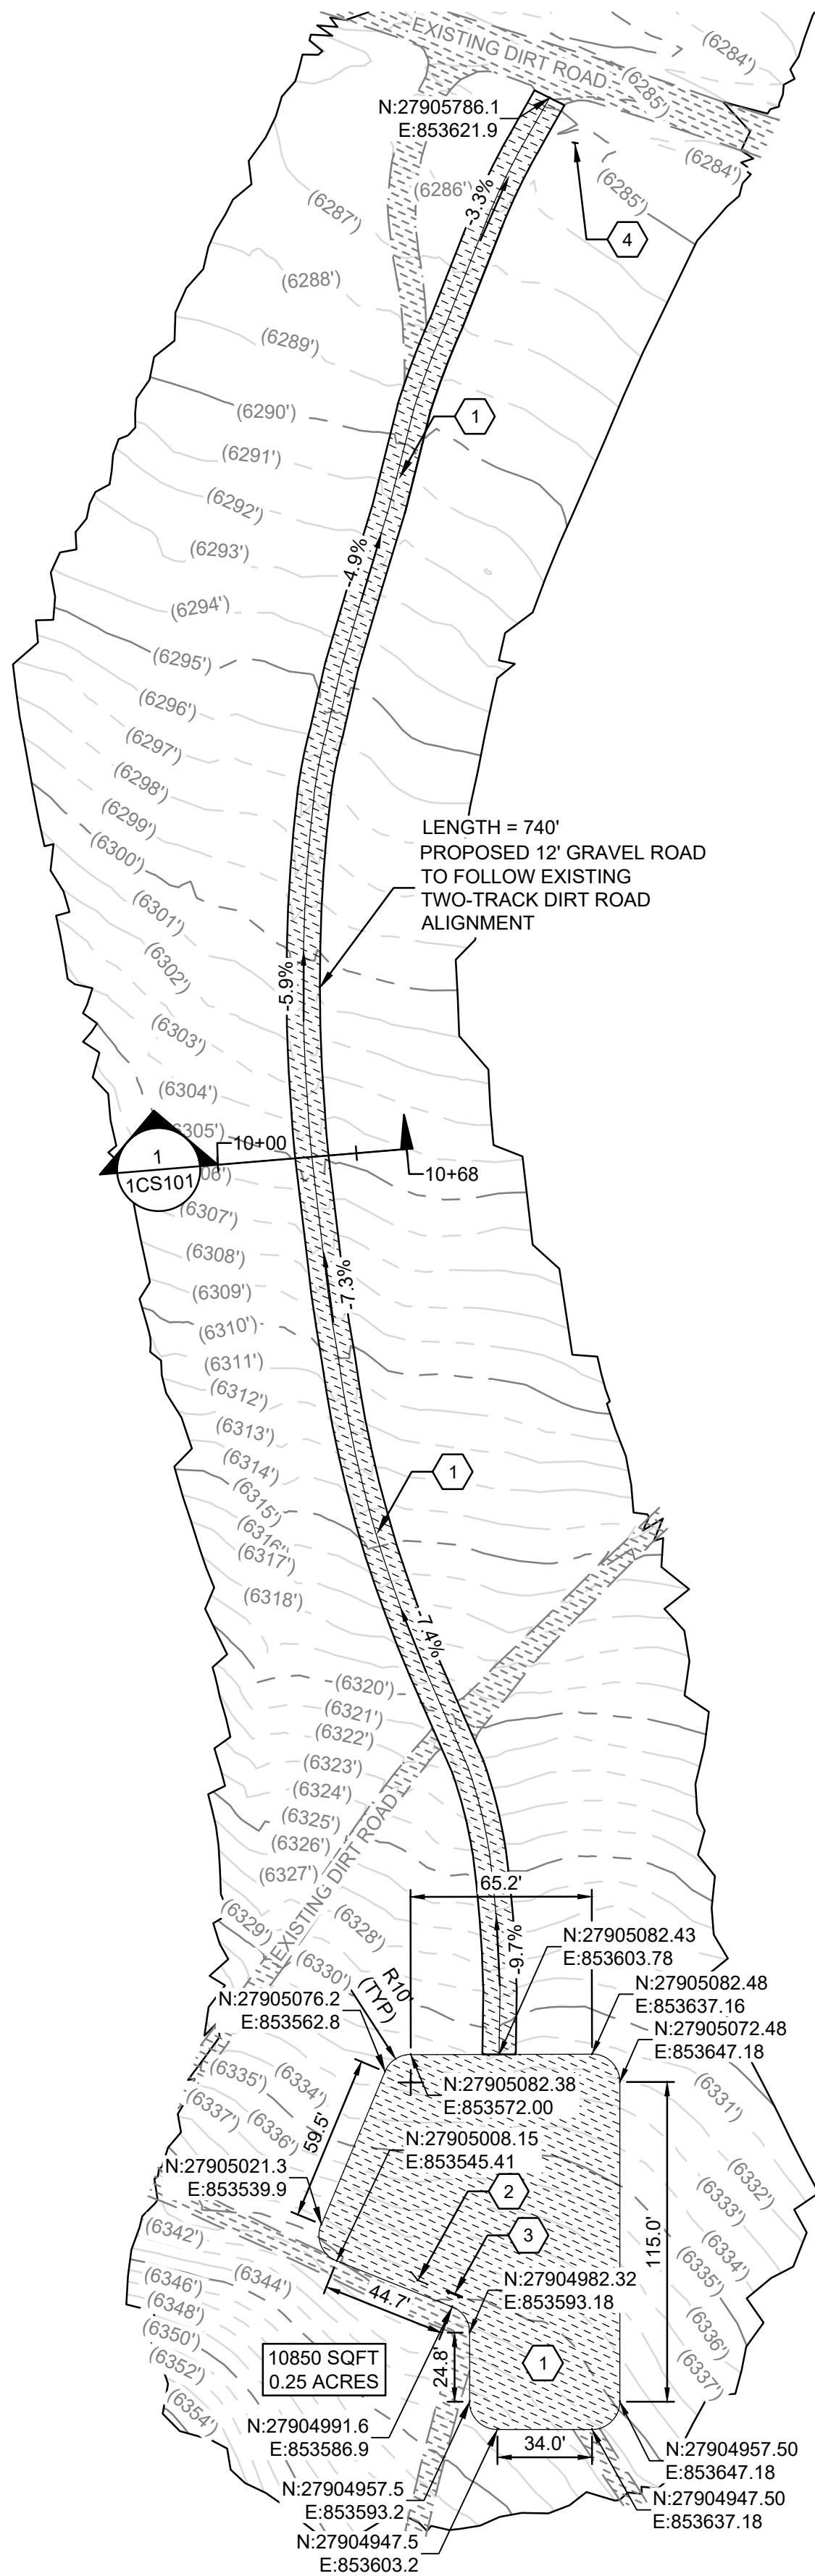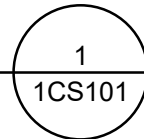

LACKAWANNA SITE PLAN

1" = 50'

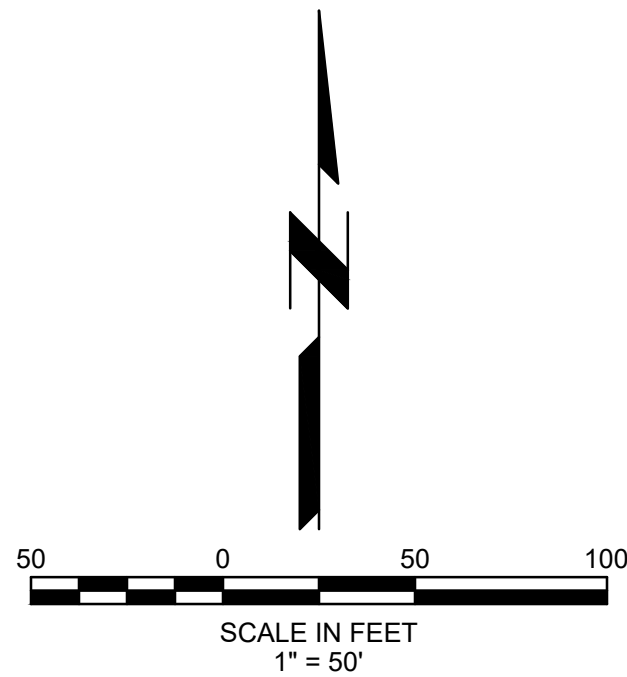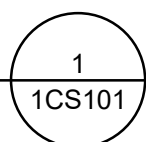


CONSTRUCTION NOTES



1	CONSTRUCT GRAVEL SURFACE PER DTL 4, DWG CD501.
2	INSTALL ROCKART KIOSK 03-420 OR APPROVED EQUIVALENT. REFER TO DTL 2, DWG CD502.
3	CONTRACTOR TO INSTALL 2 STEEL POSTS FOR "LACKAWANNA TRAILHEAD" SIGN PER DTL 4, DWG CD504. SIGN TO BE INSTALLED BY BLM.
4	CONTRACTOR TO INSTALL SINGLE BREAKAWAY SIGN POST FOR "TRAILHEAD THIS WAY" SIGN PER DTL 6, DWG CD504. SIGN TO BE INSTALLED BY BLM.

GRADING NOTES:

1. SCARIFY AND RECOMPACT GRAVEL PARKING AREA AND GRAVEL ROAD.
2. RESURFACE PARKING AREA AND GRAVEL ROAD PER DTL 4, DWG CD501.
3. MAINTAIN EXISTING GRADES.
4. DISPOSE OF EXCESS MATERIALS OFFSITE.

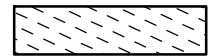

PROPOSED GRAVEL PARKING AREA AND GRAVEL ROAD

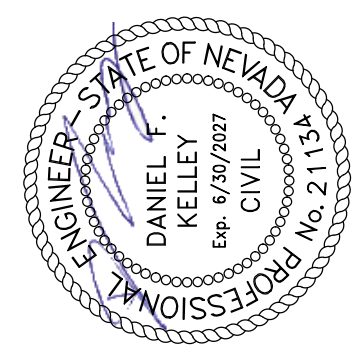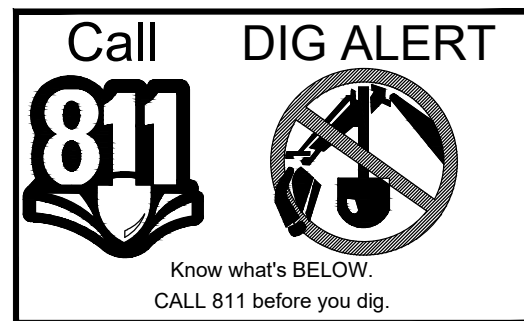

UNITED STATES DEPARTMENT OF THE INTERIOR
BUREAU OF LAND MANAGEMENT

GARNET HILL RECREATION AREA TITLE I AND II SERVICES


BUREAU OF LAND MANAGEMENT DISTRICT OFFICE
ELY, NEVADA

Project Status	Issue Date
100% CONSTRUCTION DOCUMENTS	12/16/2025
BLM Project #	140L0621D0006
Drawn By	ABROWN
Checked By	D.KELLEY

Revision Issue	Date
Description	
Rev. #	

01 - LACKAWANNA
LACKAWANNA SITE PLAN


1CS101

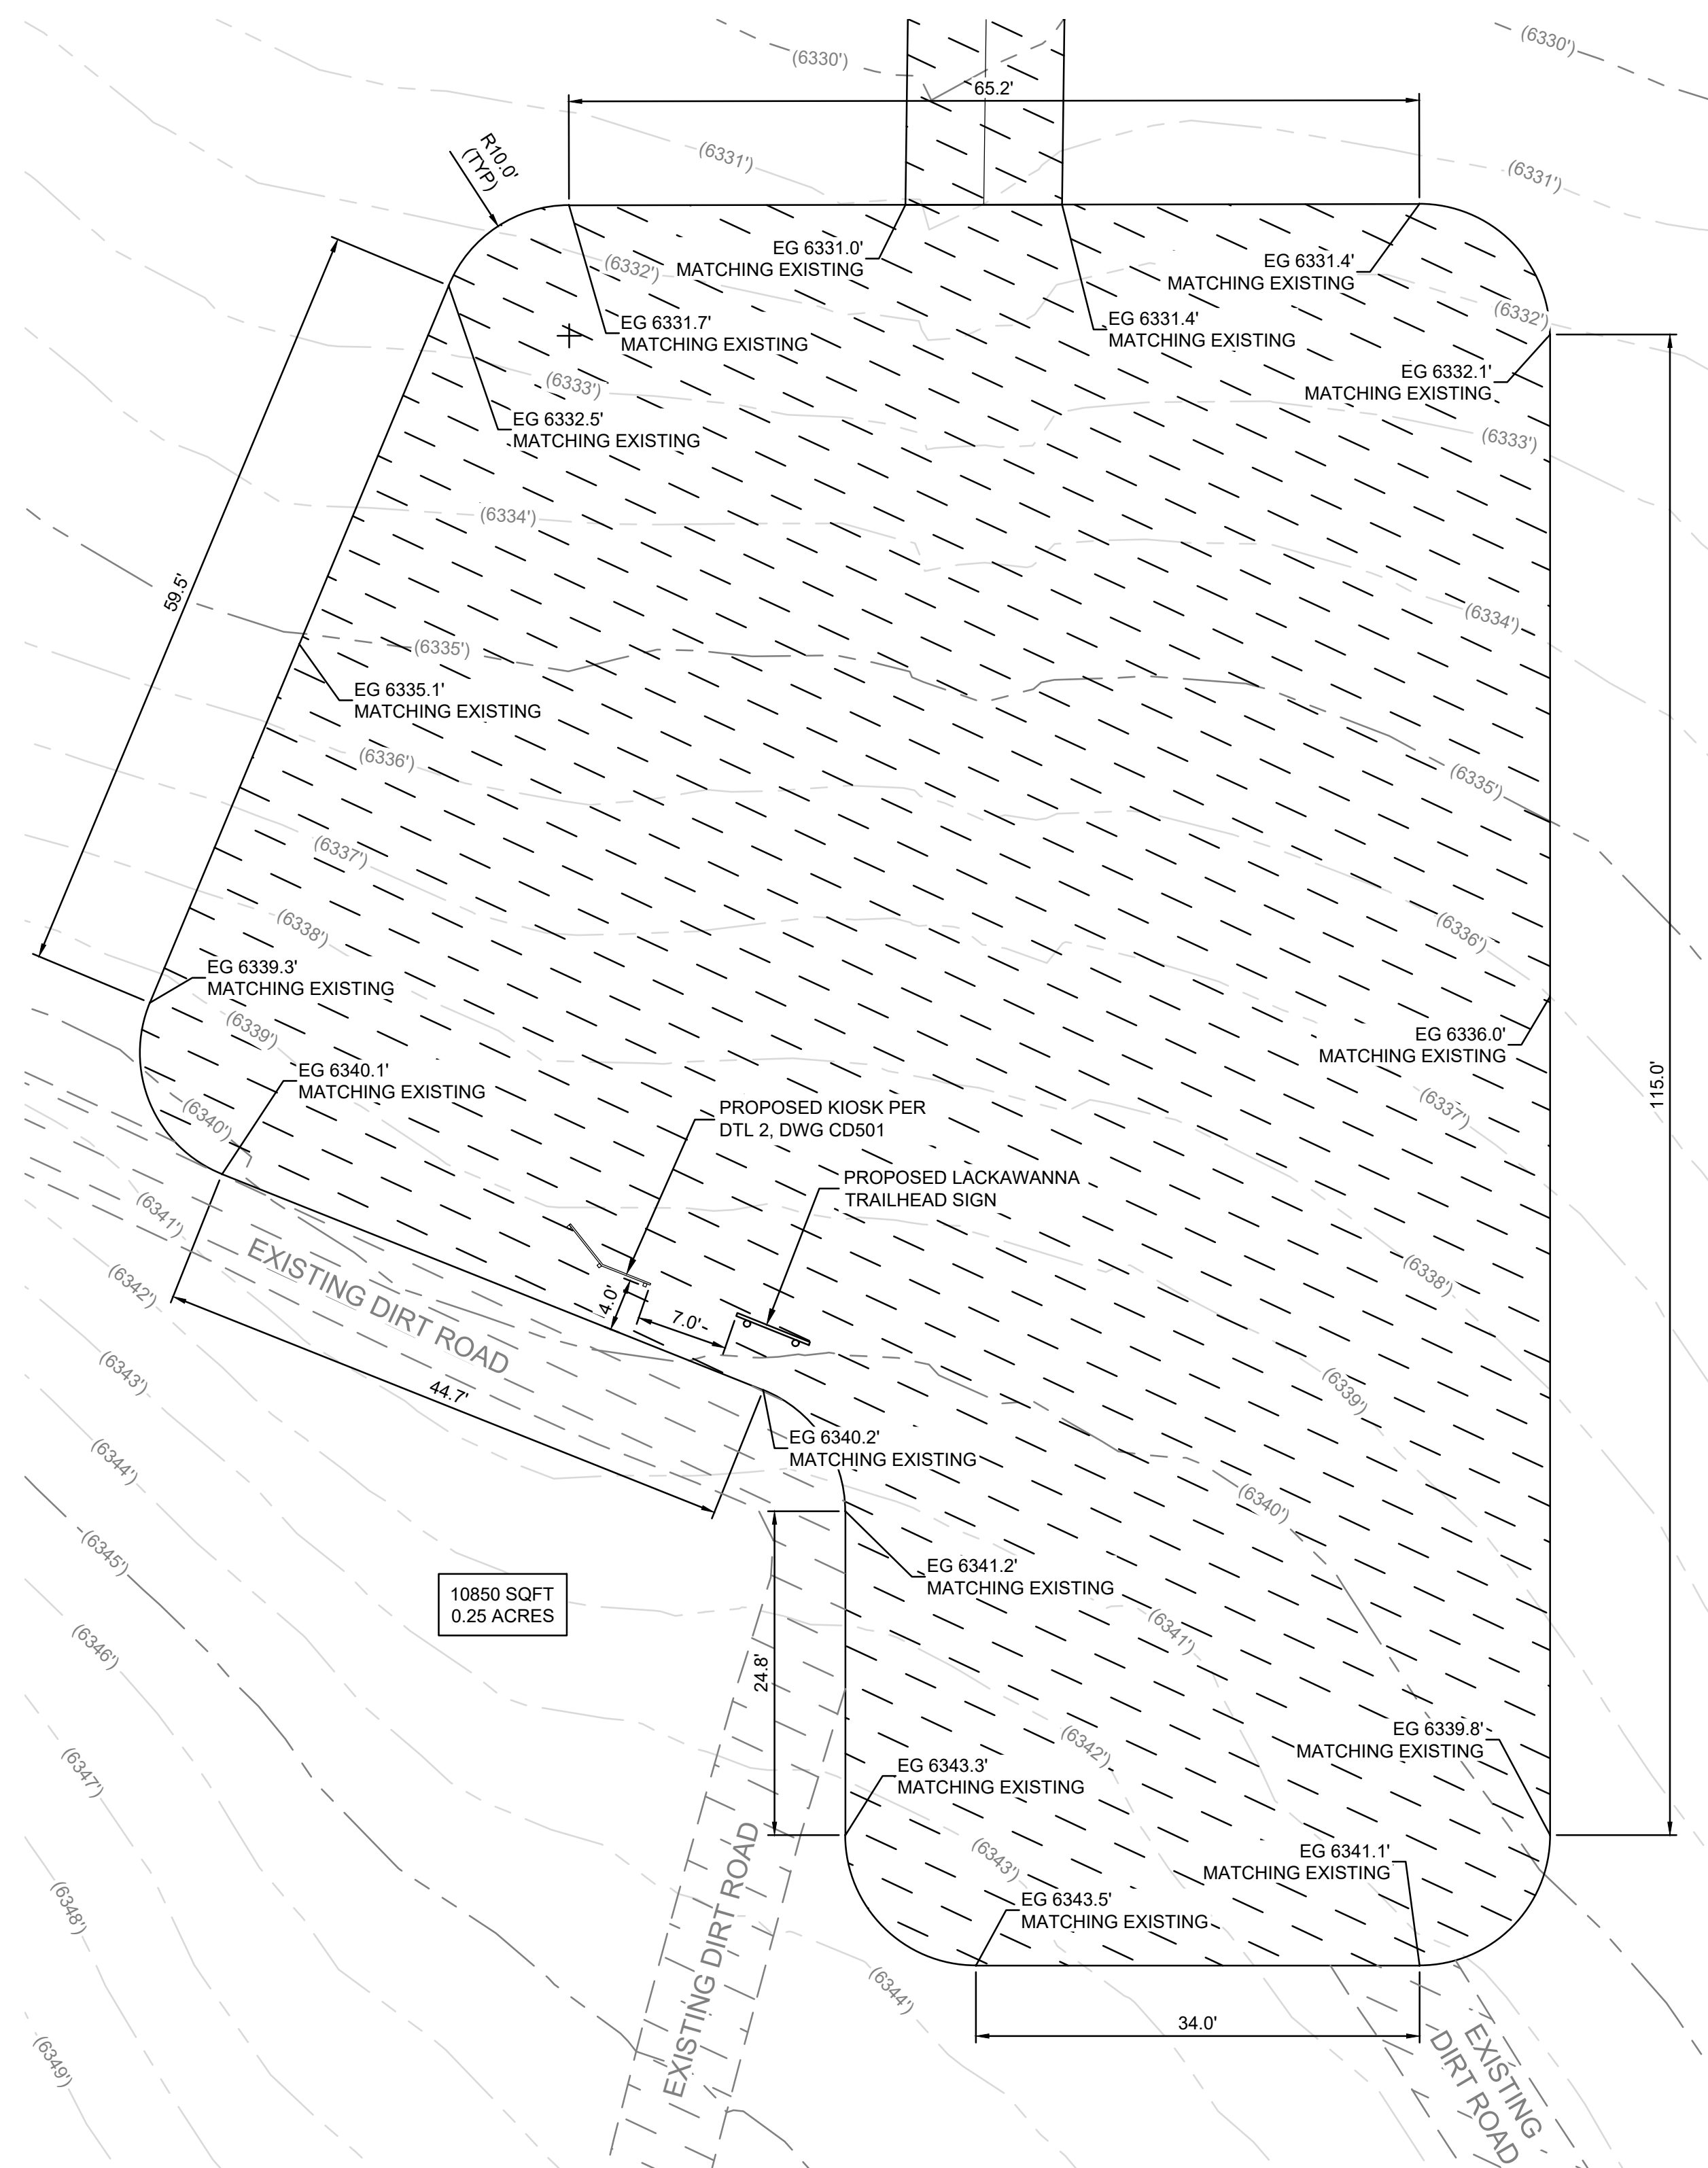

LACKAWANNA GRADING PLAN

 $1'' = 10'$

1
CG101

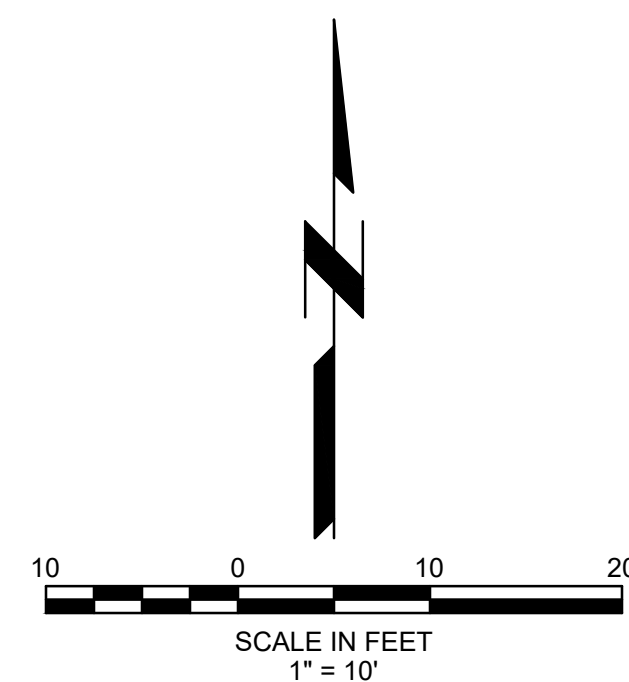


GRADING NOTES:

1. SCARIFY AND RECOMPACT GRAVEL PARKING AREA AND GRAVEL ROAD.
2. RESURFACE PARKING AREA AND GRAVEL ROAD PER DTL 4/CD501.
3. MAINTAIN EXISTING GRADES.
4. DISPOSE OF EXCESS MATERIALS OFFSITE.



PROPOSED GRAVEL PARKING AREA AND GRAVEL ROAD

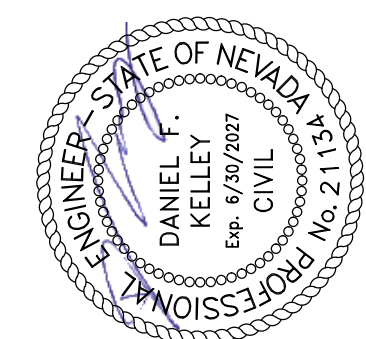

19 Dec 2025

GARNET HILL RECREATION AREA TITLE I AND II SERVICES


UNITED STATES DEPARTMENT OF THE INTERIOR
BUREAU OF LAND MANAGEMENT

BUREAU OF LAND MANAGEMENT DISTRICT OFFICE
ELY, NEVADA

Rev. #	Revision Issue Description	Project Status	Issue Date
	Date	100% CONSTRUCTION DOCUMENTS	12/16/2025
		BLM Project #	140L0621D0006
		Drawn By	A. BROWN
		Checked By	D. KELLEY

01 - LACKAWANNA
LACKAWANNA GRADING PLAN

1CG101

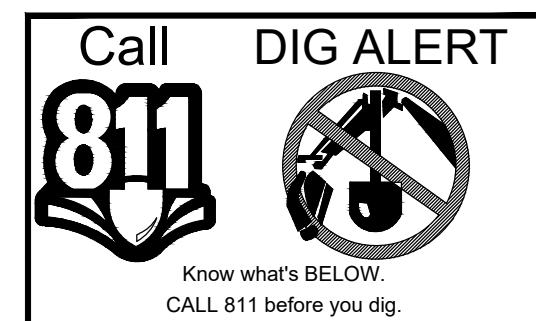

P:\Projects\BLM - NV & CA\IDOTask Orders\Task 27 - Garnet Hill Recreation Area\Task 27 - Garnet Hill Recreation Area Title I & II Services\Engineering\Drawings\Production Drawings\02 - Egan Crest Trail\HEAD0208-003-02-CR.dwg 12/16/2025 8:12 AM ABRON



50050100

SCALE IN FEET
1" = 50'

DEMOLITION NOTES

1	CLEAR AND GRUB
2	REMOVE EXISTING SHADE STRUCTURE
3	REMOVE EXISTING KIOSK

CLEAR AND GRUB LIMITS (306,900 SF)

EGAN CREST DEMOLITION PLAN
1" = 50'

1
2CR101

Call

811

Know what's BELOW.
CALL 811 before you dig.

DIG ALERT

NATIONAL SYSTEM OF PUBLIC LANDS
U.S. DEPARTMENT OF THE INTERIOR
BUREAU OF LAND MANAGEMENT

U.S. DEPARTMENT OF THE INTERIOR
6981 3
MARCH 3
U.S. DEPARTMENT OF THE INTERIOR

ENGINEER - STATE OF NEVADA
DANIEL F. KELLEY
No. 21134
Exp. 12/31/2027
PROFESSIONAL CIVIL

19 Dec 2025

UNITED STATES DEPARTMENT OF THE INTERIOR
BUREAU OF LAND MANAGEMENT

**GARNET HILL RECREATION AREA TITLE I
AND II SERVICES**

BUREAU OF LAND MANAGEMENT DISTRICT OFFICE
ELY, NEVADA


Project Status
100% CONSTRUCTION DOCUMENTS
BLM Project #
Drawn By
Checked By

Issue Date
12/16/2025
140L0621D0006
ABRON
D. KELLEY

02 - EGAN CREST
EGAN CREST DEMOLITION PLAN

2CR101

P:\Projects\BLM - NV & CA IDIO\Task Orders\Task 27 - Garnet Hill Recreation Area Title I & II Services\Engineering\Drawings\Production Drawings\02 - EGAN CREST TRAILHEAD\0208-003-02-02-02.dwg 12/16/2025 8:16 AM KMLVESTUTO

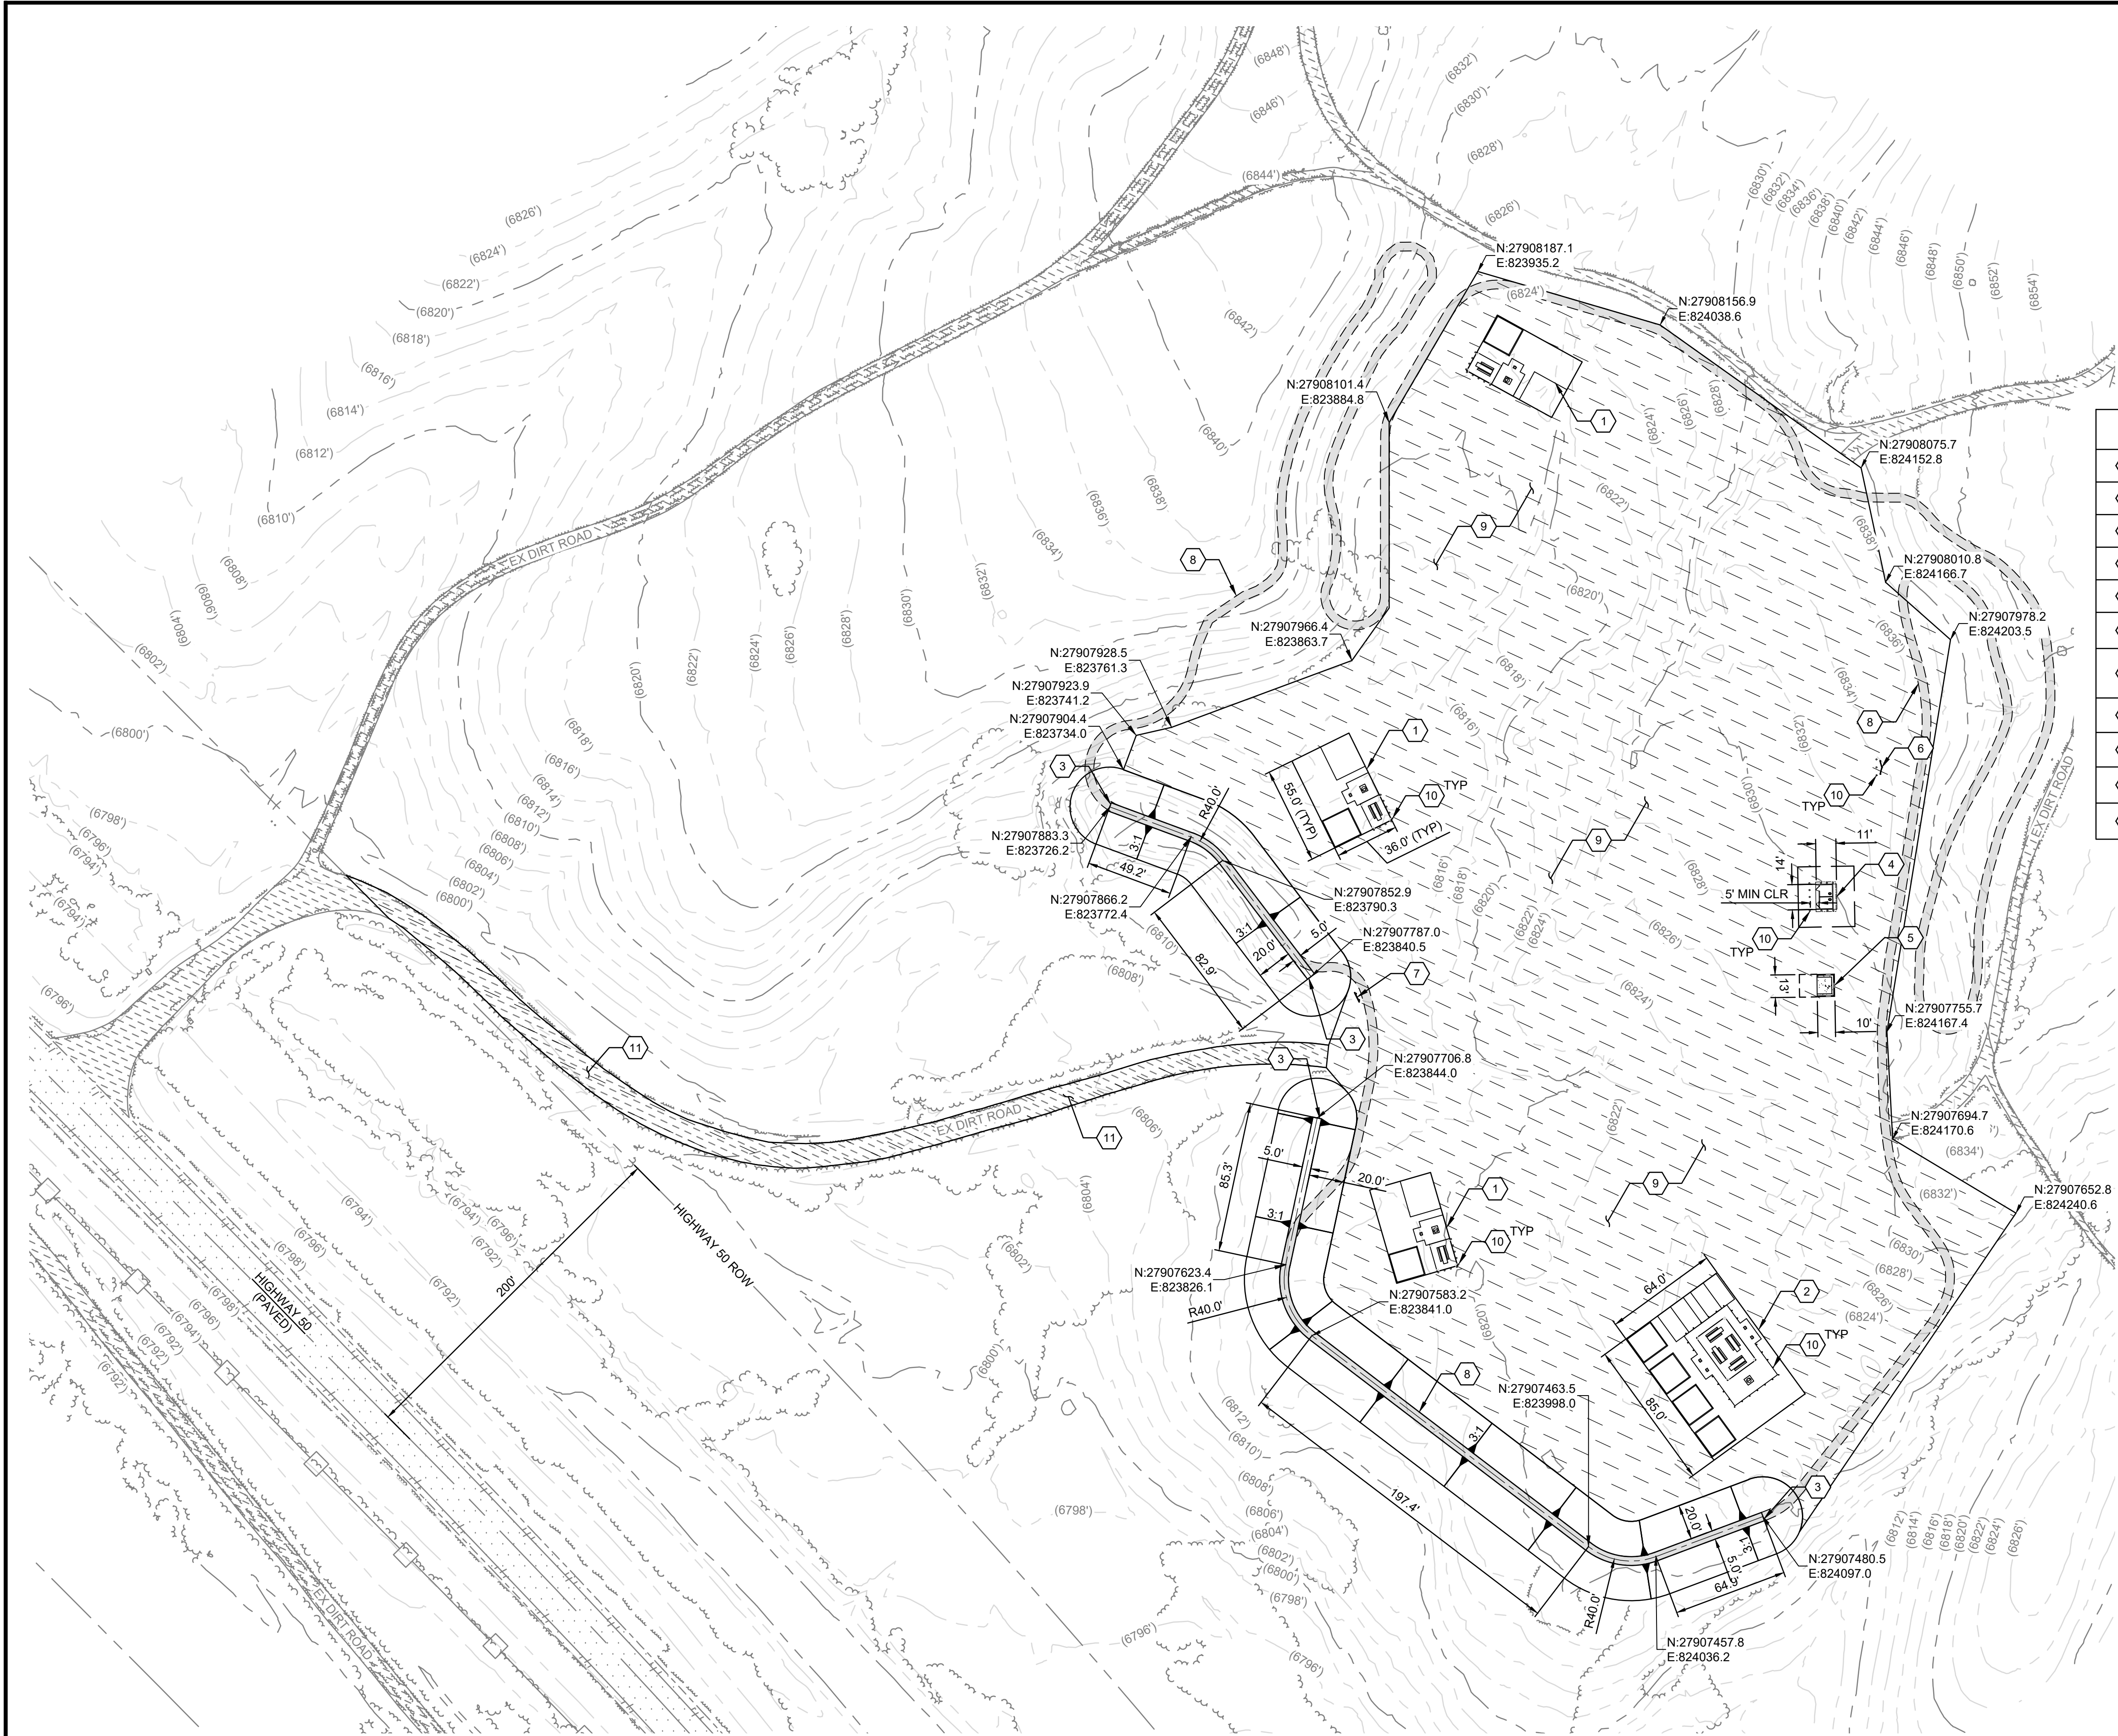

CONSTRUCTION NOTES	
1	CONSTRUCT INDIVIDUAL CAMPSITE PER DTL 1, DWG CD503.
2	CONSTRUCT GROUP CAMPSITE PER DTL 2, DWG CD503.
3	CONSTRUCT BERM PER DTL 1, DWG 2CG101.
4	INSTALL DOUBLE VAULT TOILET PER DTL 1, DWG CD502.
5	CONSTRUCT TRASH ENCLOSURE PER DTL 2, DWG CD505.
6	INSTALL ROCKART KIOSK 03-441 OR APPROVED EQUIVALENT. REFER TO DTL 2, DWG CD502.
7	CONTRACTOR TO INSTALL 3 STEEL POSTS FOR "EGAN CREST TRAILHEAD" SIGN PER DTL 5, DWG CD504. SIGN TO BE INSTALLED BY BLM.
8	CONSTRUCT 5' WIDE NATURAL SURFACE MINI BIKE TRAIL.
9	CONSTRUCT GRAVEL SURFACE PER DTL 4, CD501.
10	INSTALL VEHICLE PROTECTION BOLLARDS WITH ADA COMPLIANCE PER DTL 6, DWG CD501.
11	IMPROVE GRAVEL ROAD PER DTL 4, DWG CD501. MAINTAIN EXISTING ROAD WIDTH.

EGAN CREST SITE PLAN
1" = 50'

1
2CS101

Call

811

Know what's BELOW.
CALL 811 before you dig.

DIG ALERT

NATIONAL SYSTEM OF PUBLIC LANDS
U.S. DEPARTMENT OF THE INTERIOR
BUREAU OF LAND MANAGEMENT

U.S. DEPARTMENT OF THE INTERIOR
6981 S. MARCH 3, 1927

ENGINEER
STATE OF NEVADA
DANIEL F. KELLEY
No. 21134
Exp. 12/31/2027
CIVIL

19 Dec 2025

UNITED STATES DEPARTMENT OF THE INTERIOR
BUREAU OF LAND MANAGEMENT

**GARNET HILL RECREATION AREA TITLE I
AND II SERVICES**

BUREAU OF LAND MANAGEMENT DISTRICT OFFICE
ELY, NEVADA

Issue Date
12/16/2025

Project Status
100% CONSTRUCTION DOCUMENTS

Revision Issue
Description

Date

Rev. #

14010621D0006

BLM Project #



Drawn By
ABROWN

Checked By
D.KELLEY

02 - EGAN CREST
EGAN CREST SITE PLAN

2CS101


P:\Projects\BLM - NV & CA IDIO\Task Orders\Task 27 - Garnet Hill Recreation Area Title I & II Services\Engineering\Drawings\Production Drawings\02 - EGAN CREST TRAIL\HEAD008-003-02-CG.dwg 12/16/2025 8:13 AM KMA\VESTUTO

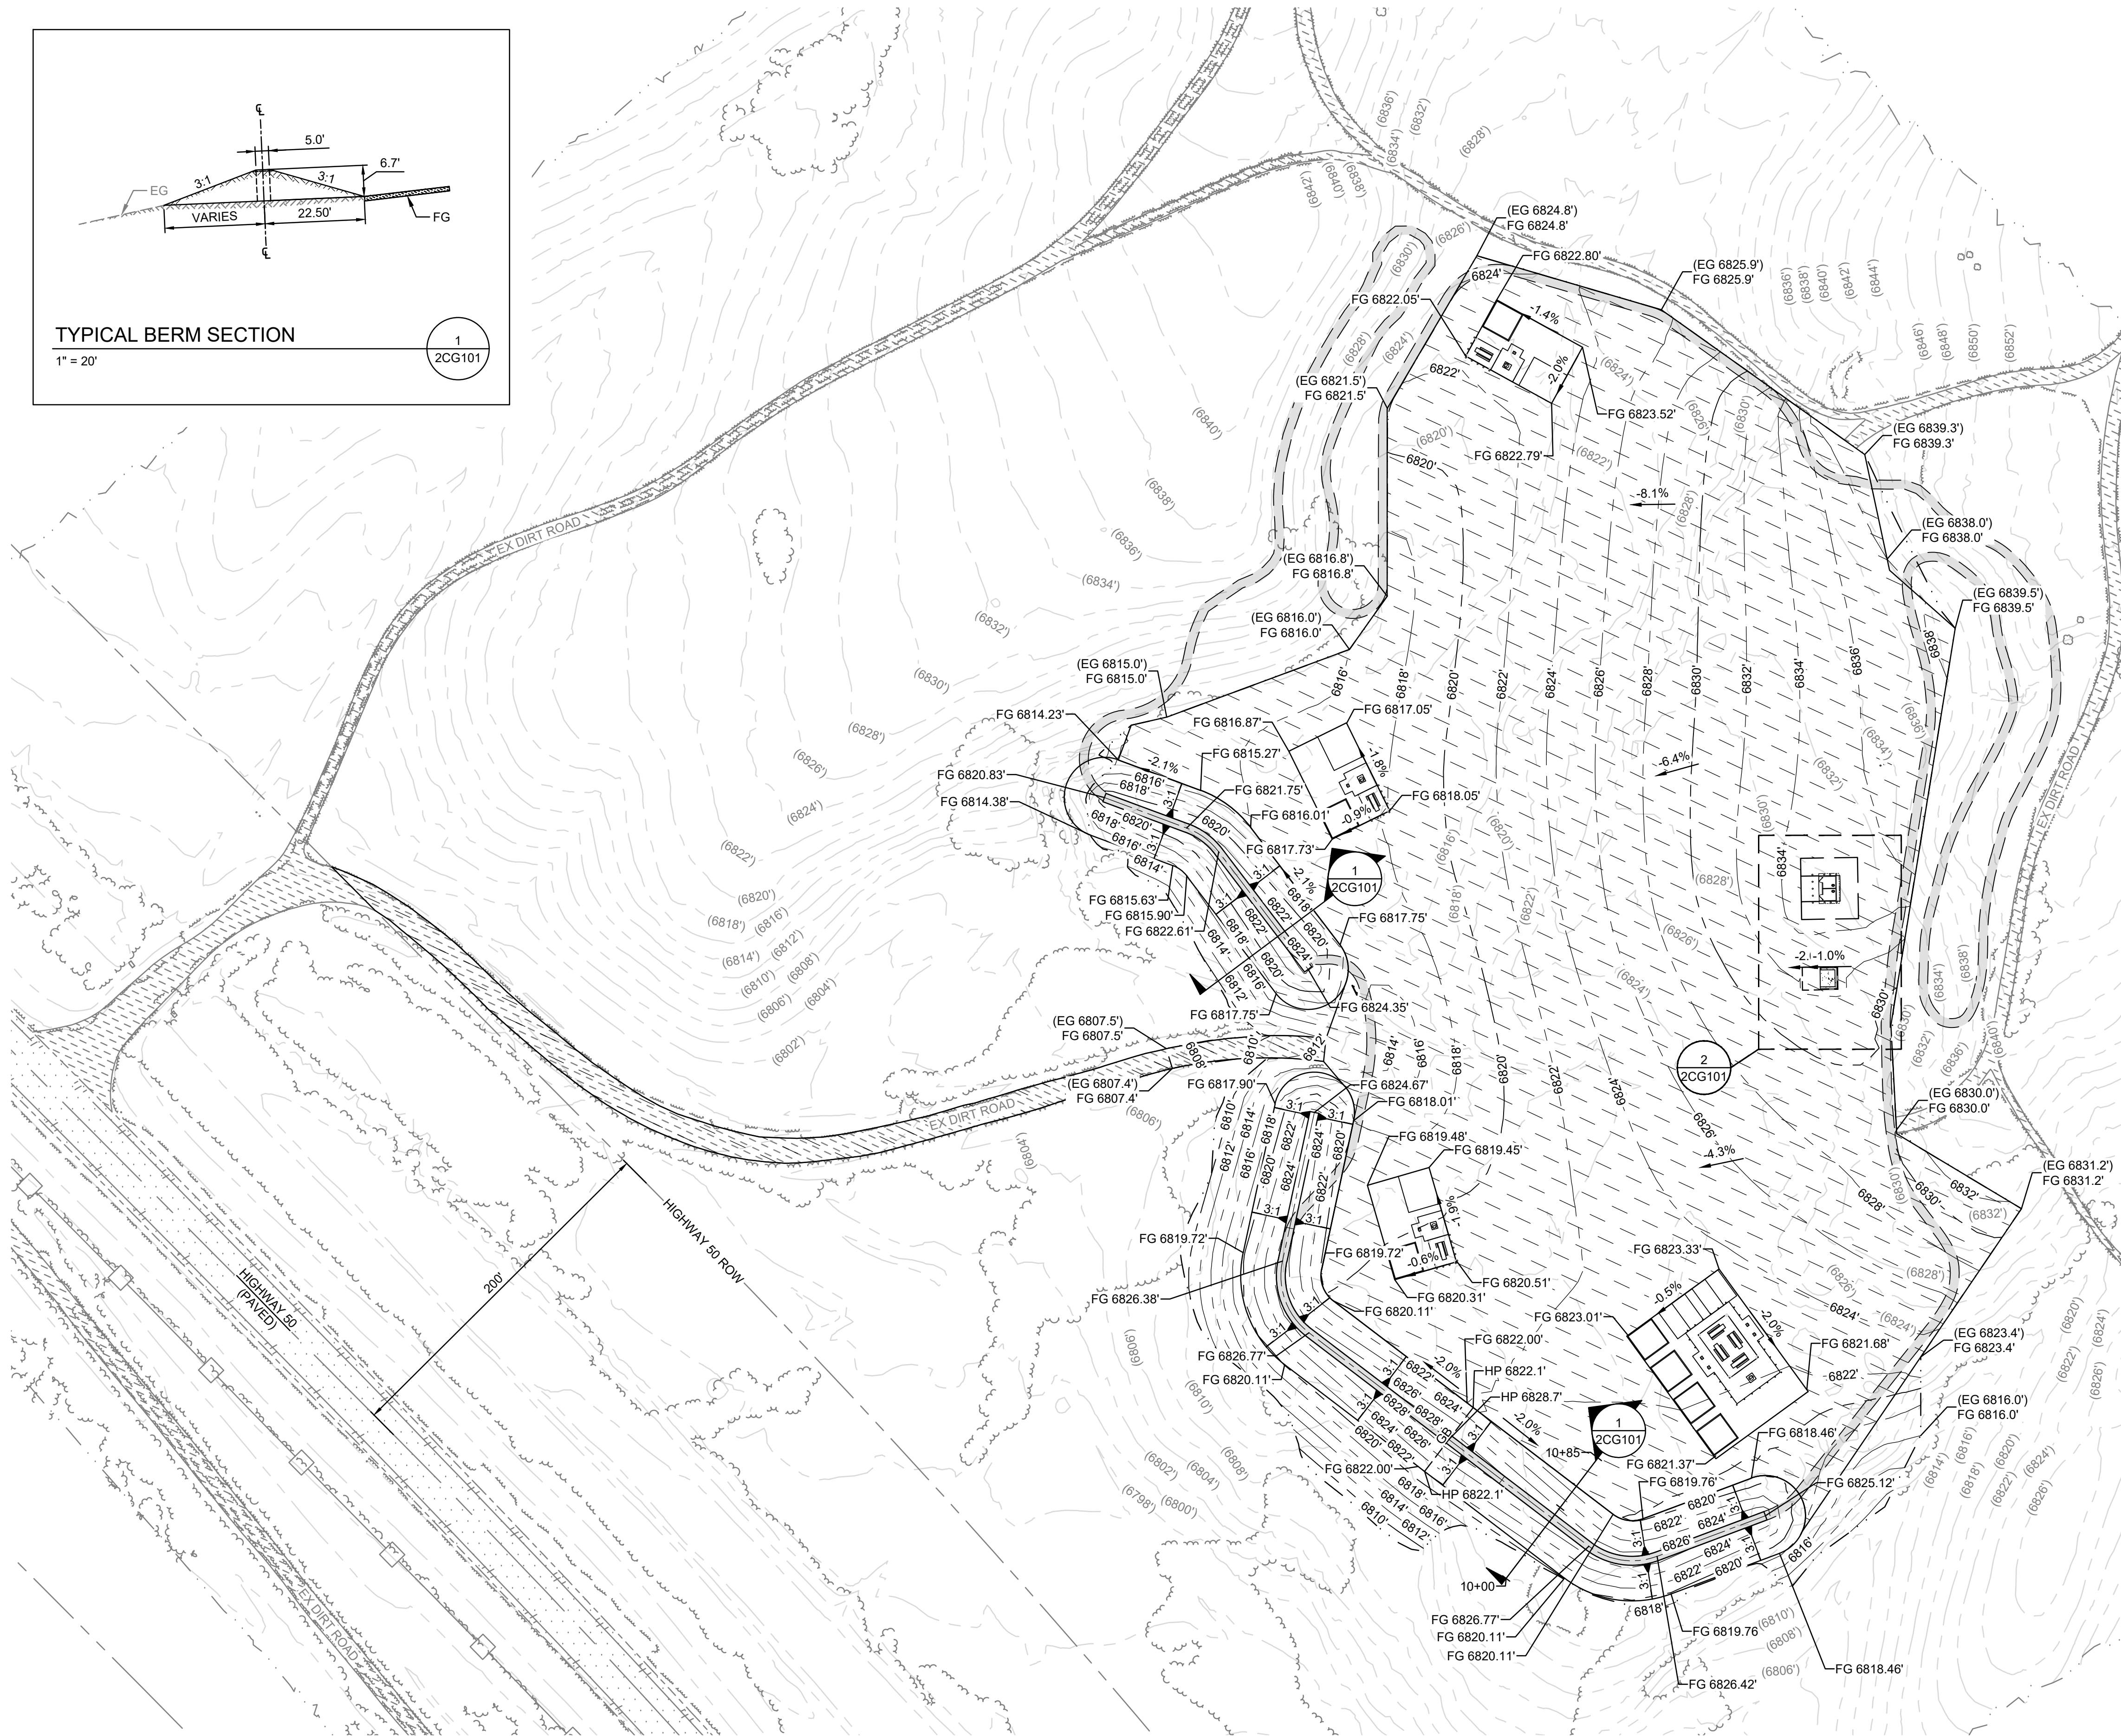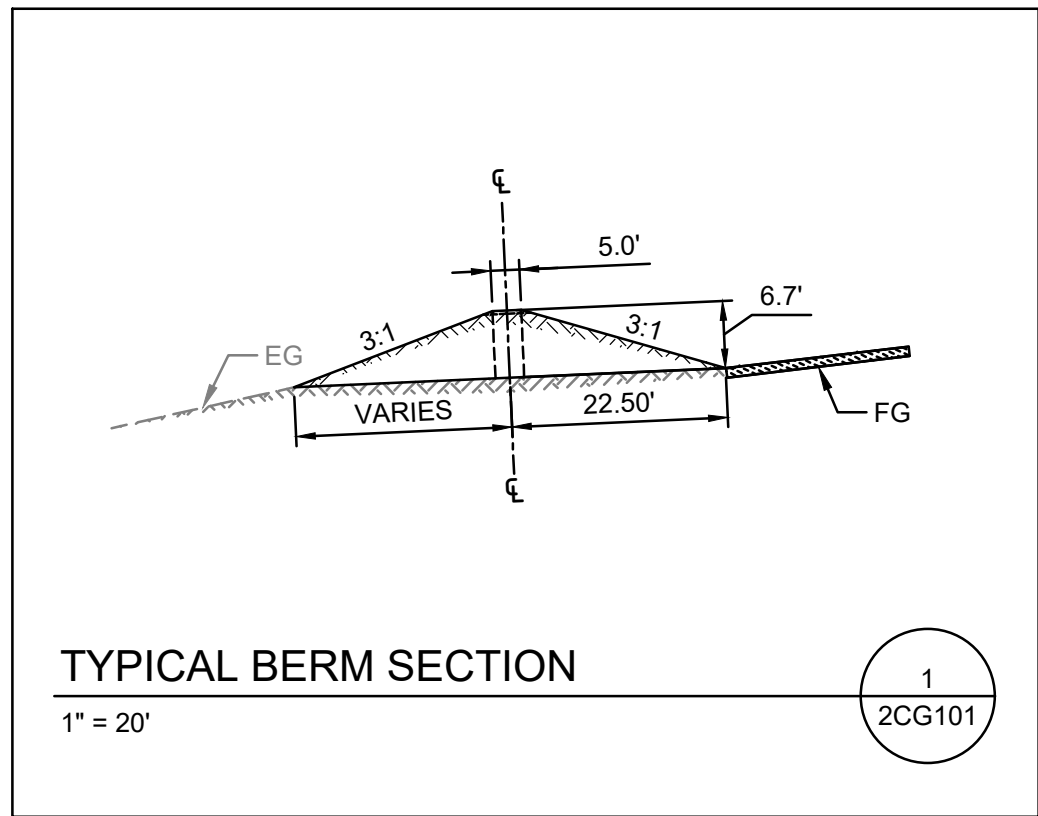


EGAN CREST GRADING PLAN

1" = 50'

1
2CG101

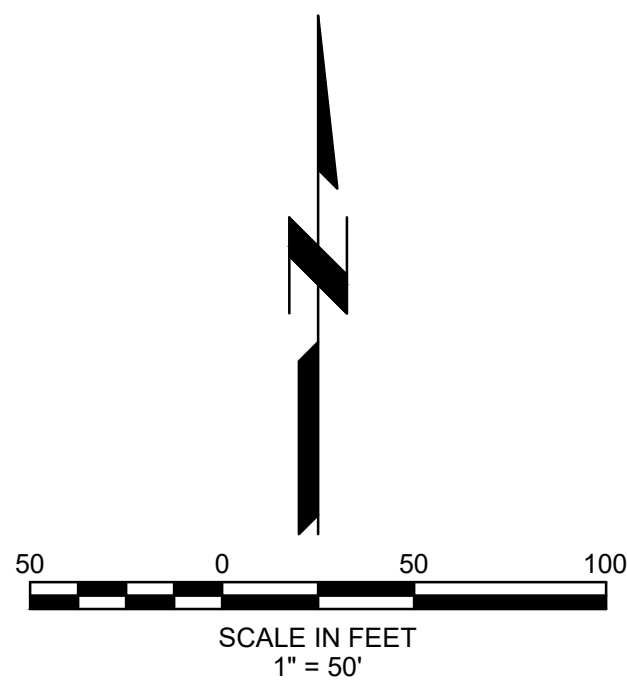


CUT/FILL VOLUMES	
CUT:	4,100 CY
FILL:	15,200 CY
NET:	11,100 CY (FILL)

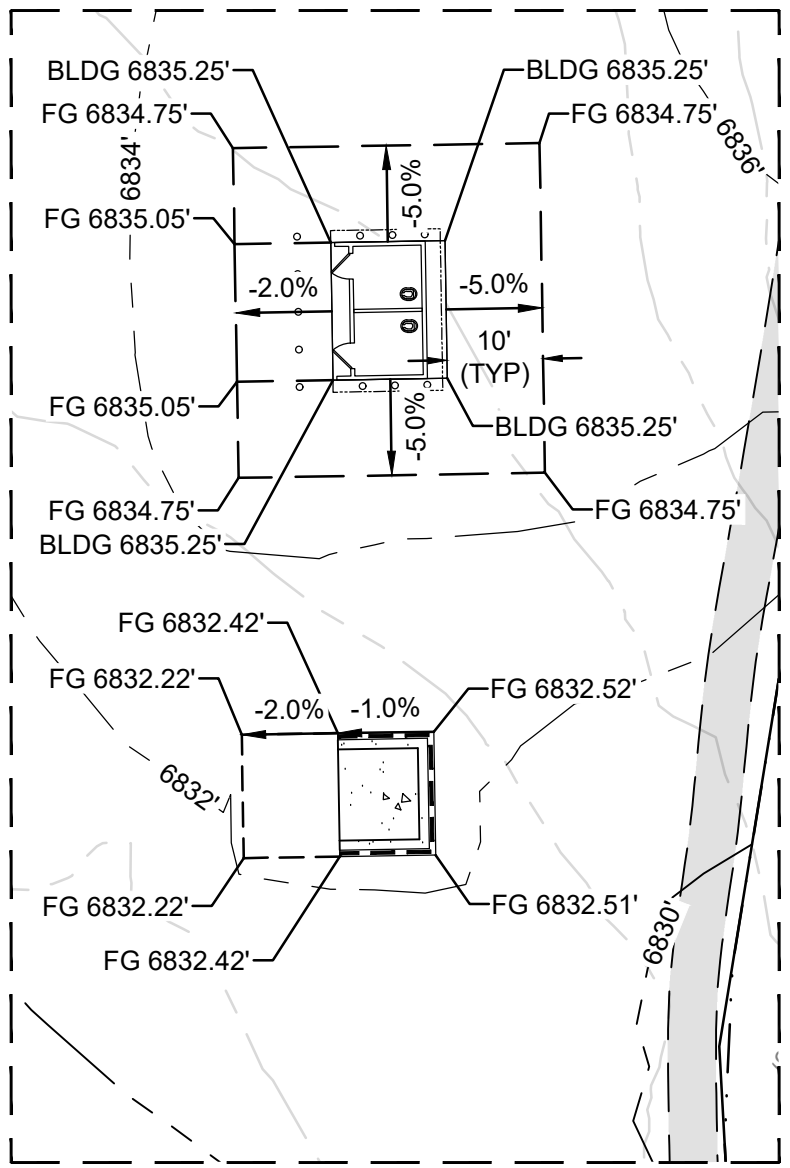

ENLARGED GRADING PLAN

1" = 20'

2
2CG101

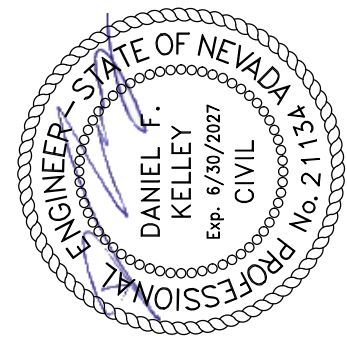

UNITED STATES DEPARTMENT OF THE INTERIOR
BUREAU OF LAND MANAGEMENT

GARNET HILL RECREATION AREA TITLE I AND II SERVICES

BUREAU OF LAND MANAGEMENT DISTRICT OFFICE
ELY, NEVADA



Issue Date	12/16/2025
Project Status	100% CONSTRUCTION DOCUMENTS
BLM Project #	140L0621D0006
Drawn By	ABROWN
Checked By	D.KELLEY
Revision Issue	
Description	
Rev. #	


02 - EGAN CREST
EGAN CREST GRADING PLAN

2CG101

19 Dec 2025

P:\Projects\BLM - NV & CA\IDOTask Orders\Task 27 - Garnet Hill Recreation Area Title I & II Services\Engineering\Drawings\Production Drawings\03 - KEYSTONE JUNCTION PARKING LOT\2025-03-03-CR.dwg 12/16/2025 8:15 AM KMAL\VESTUTO

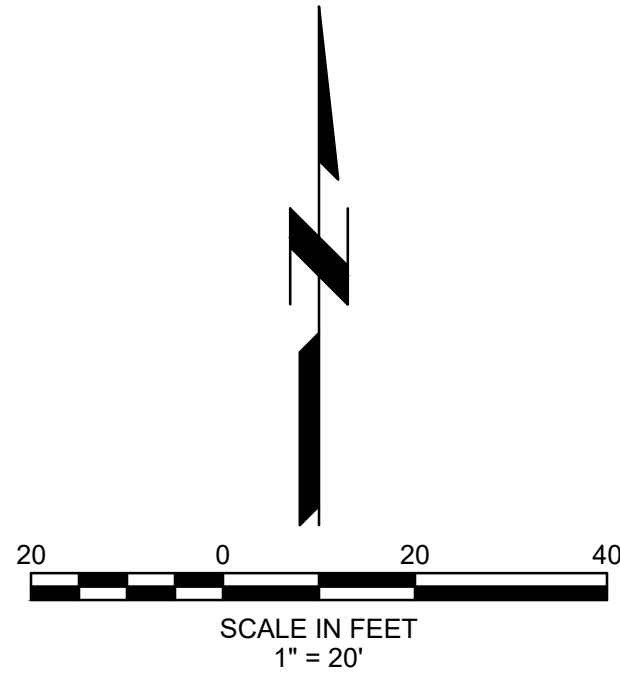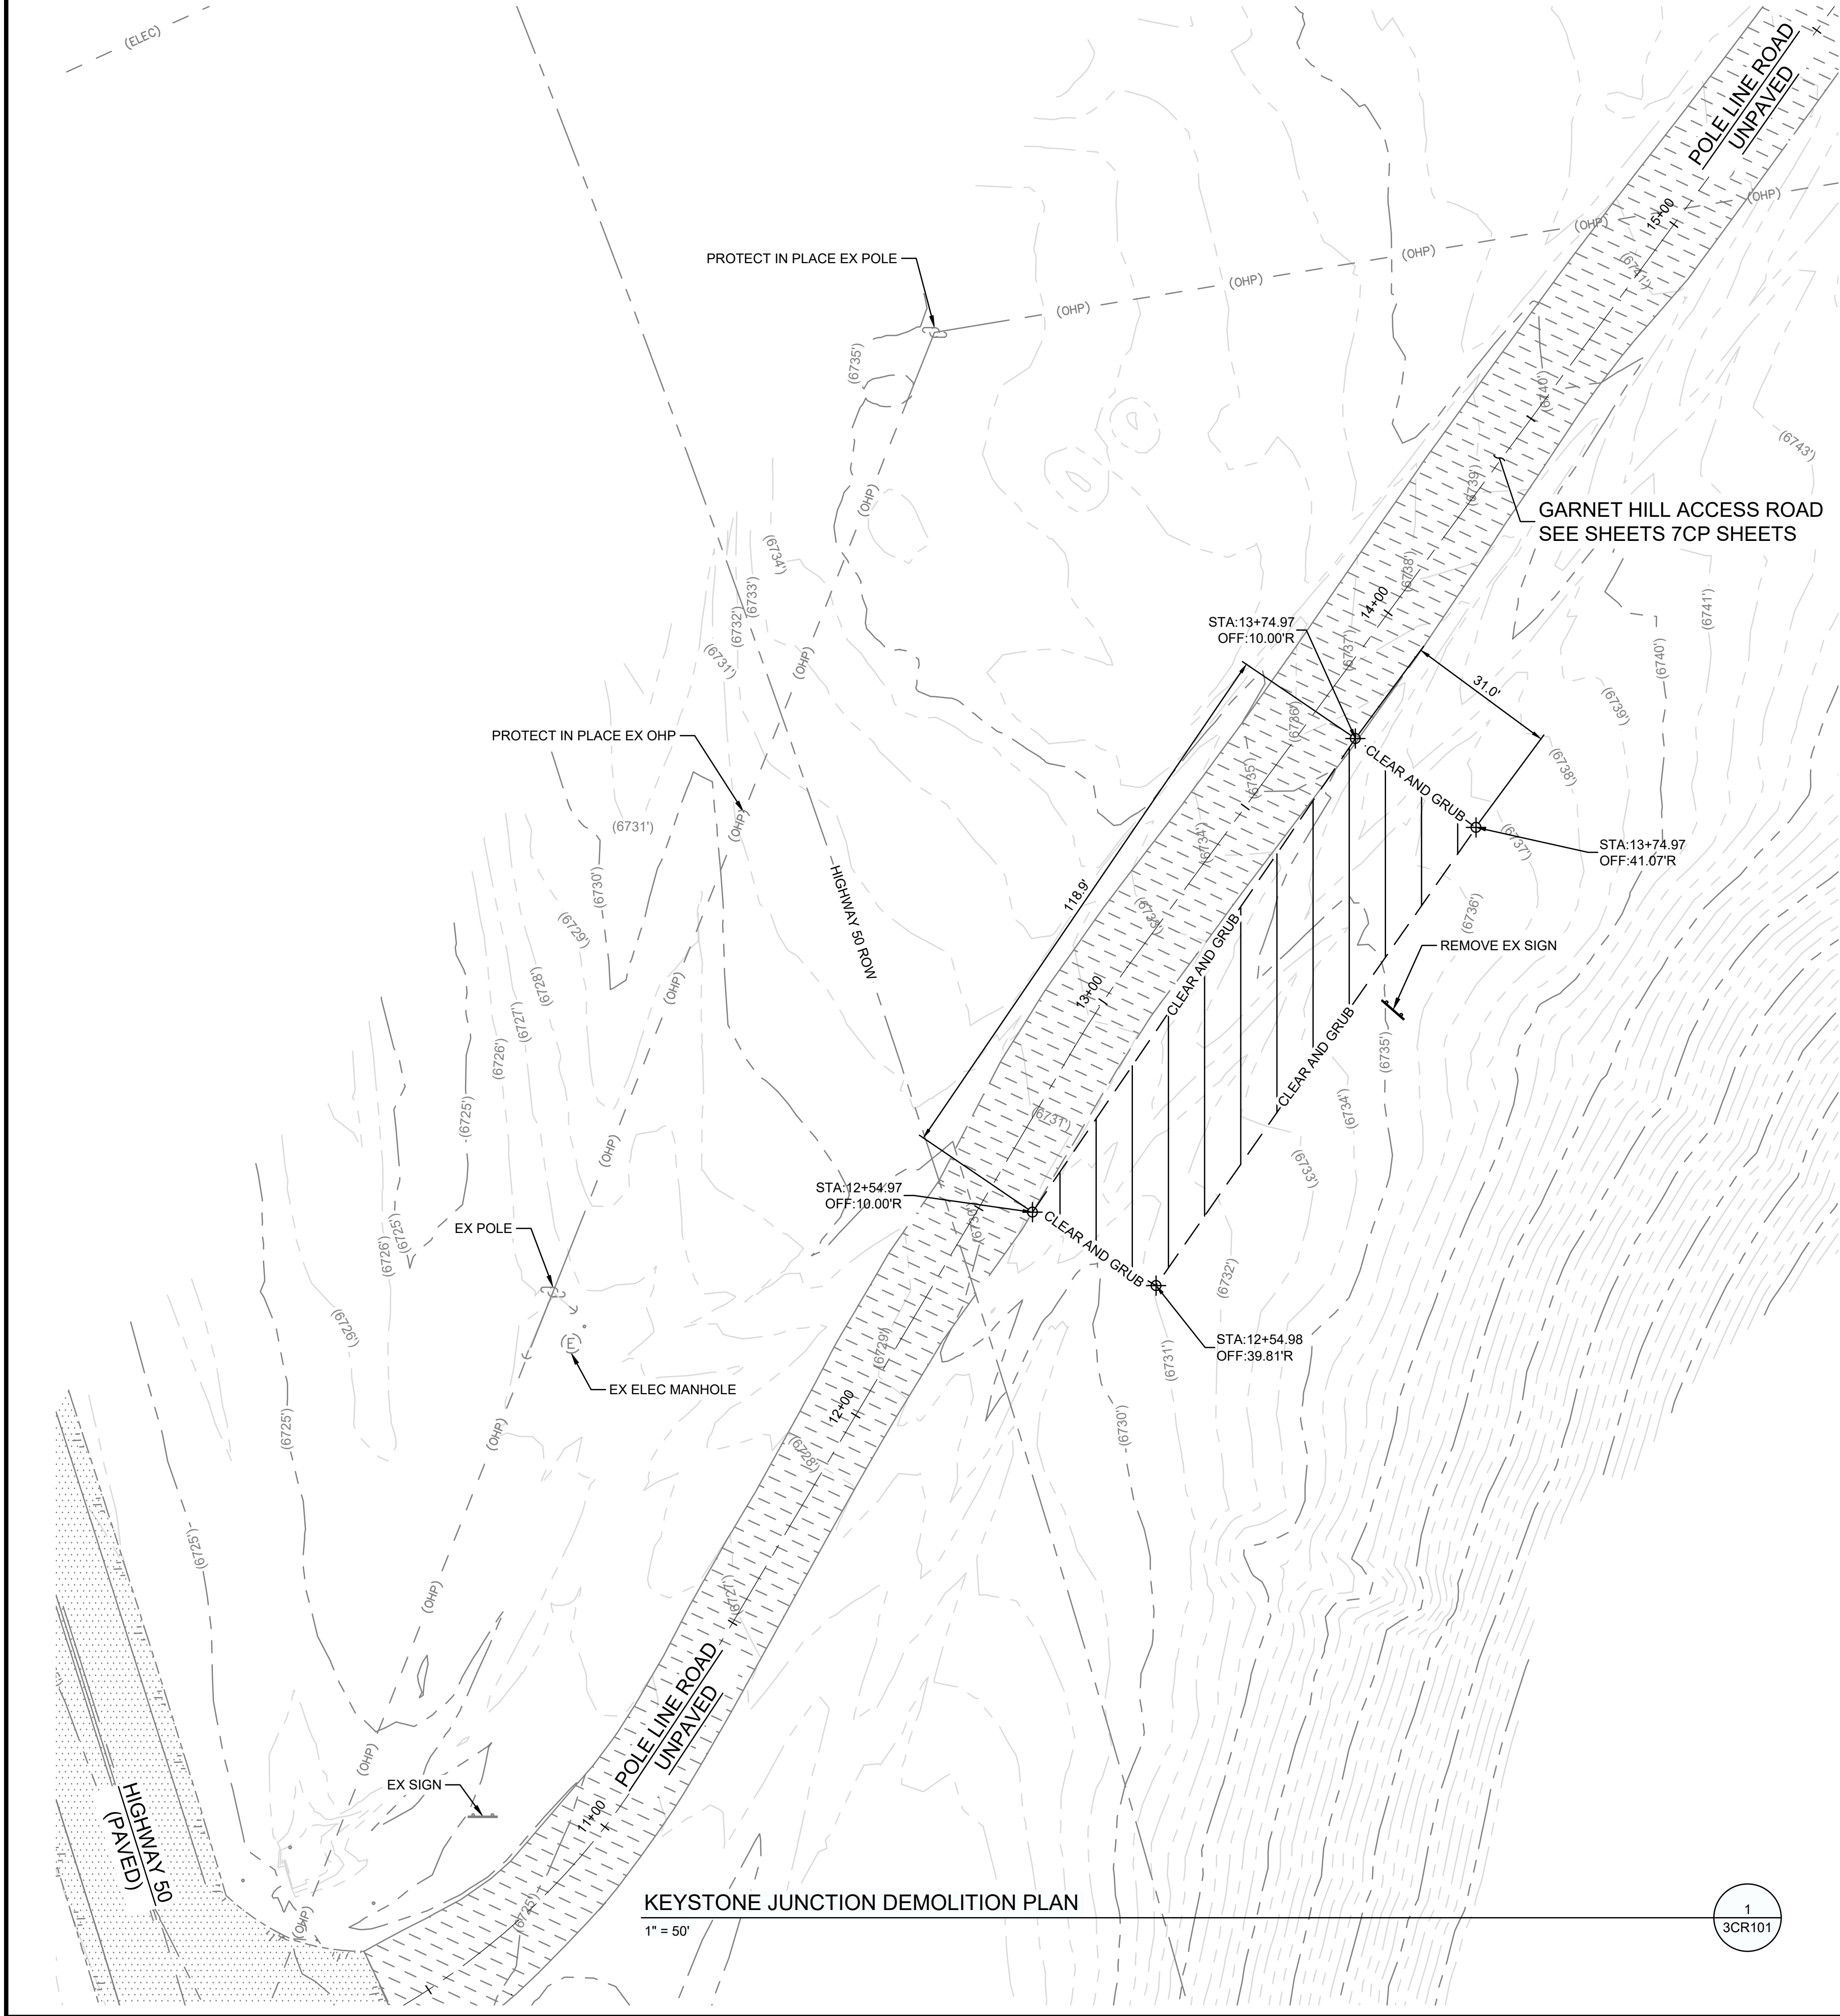

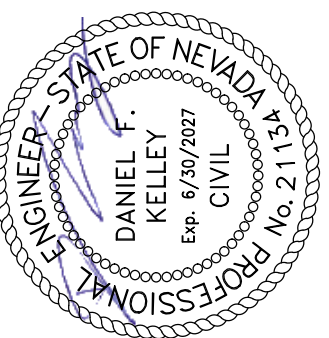

UNITED STATES DEPARTMENT OF THE INTERIOR
BUREAU OF LAND MANAGEMENT

GARNET HILL RECREATION AREA TITLE I AND II SERVICES

BUREAU OF LAND MANAGEMENT DISTRICT OFFICE
ELY, NEVADA


Project Status	Issue Date
100% CONSTRUCTION DOCUMENTS	12/16/2025
BLM Project #	140L0621D0006
Drawn By	ABROWN
Checked By	D.KELLEY

Revision Issue	Date
Description	
Rev. #	

03 - KEYSTONE JUNCTION
KEYSTONE DEMOLITION PLAN


3CR101

P:\Projects\BLM - NV & CA\IDOT\Task Orders\Task 27 - Garnet Hill Recreation Area Title I & II Services\Engineering\Drawings\Production Drawings\03 - KEYSTONE JUNCTION PARKING LOT\2025-03-03-CS.dwg 12/16/2025 8:13 AM KMA\VESTUTO

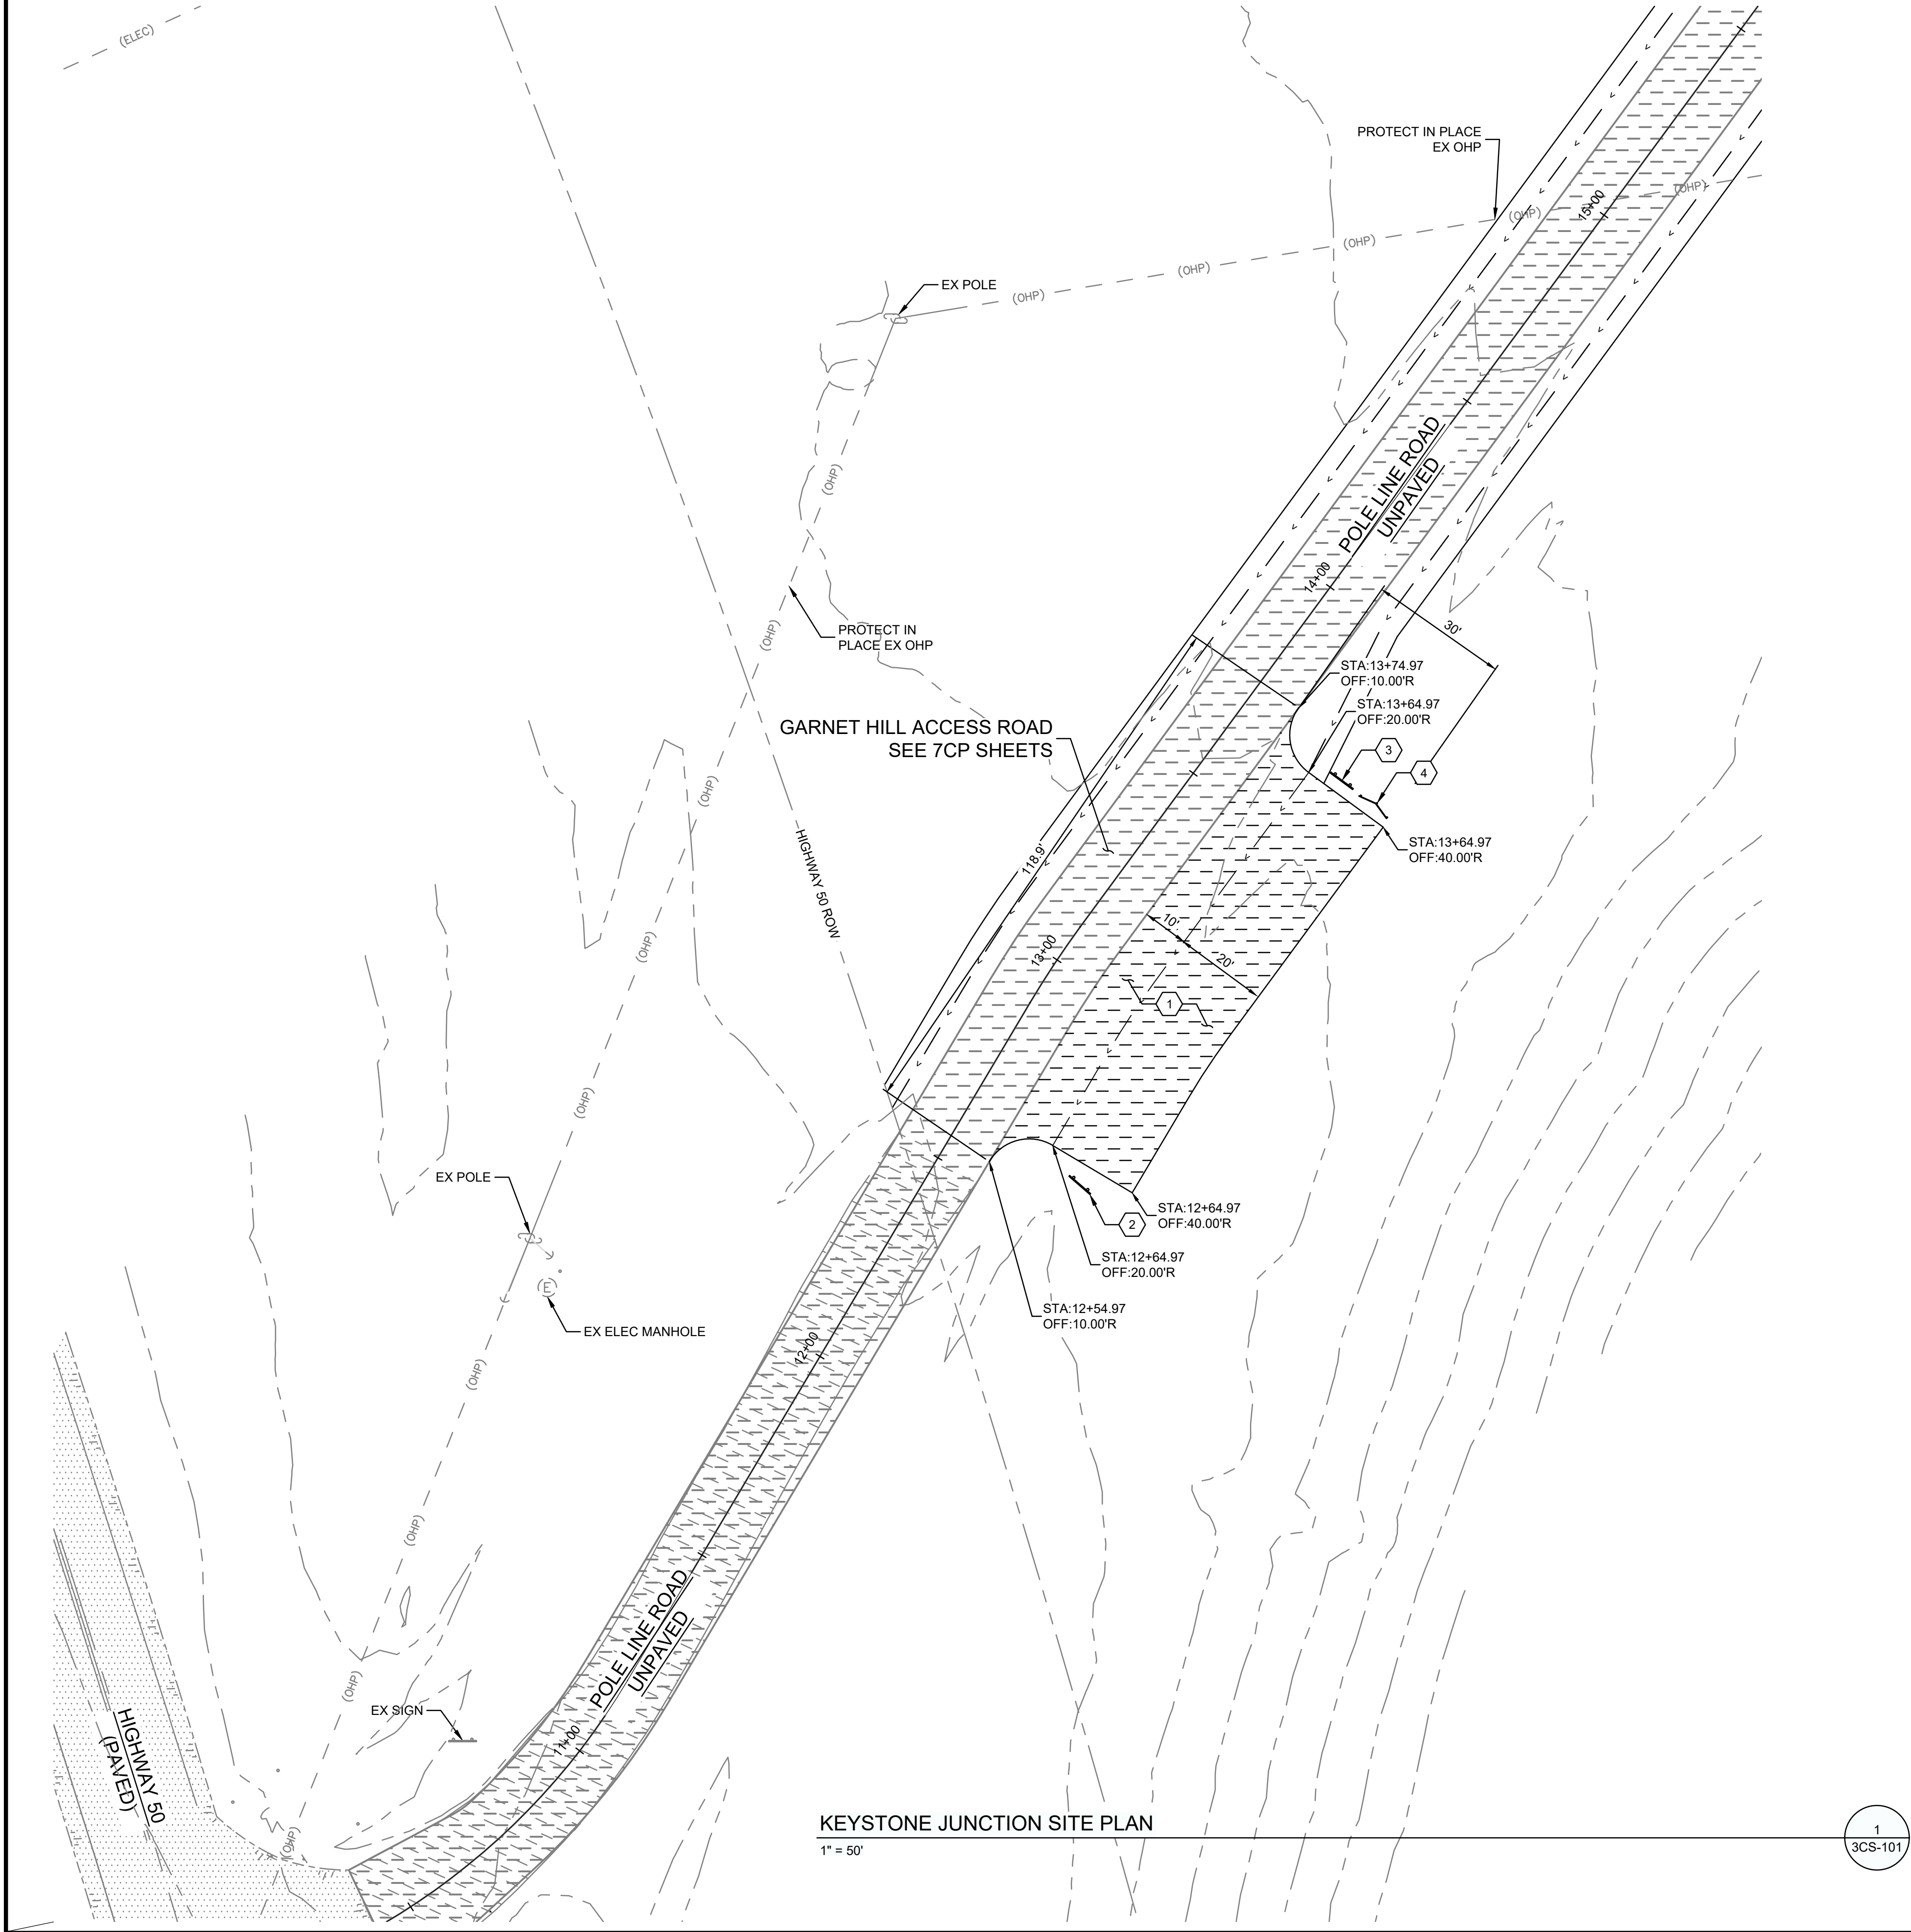


KEYSTONE JUNCTION SITE PLAN
1" = 50'

1
3CS-101

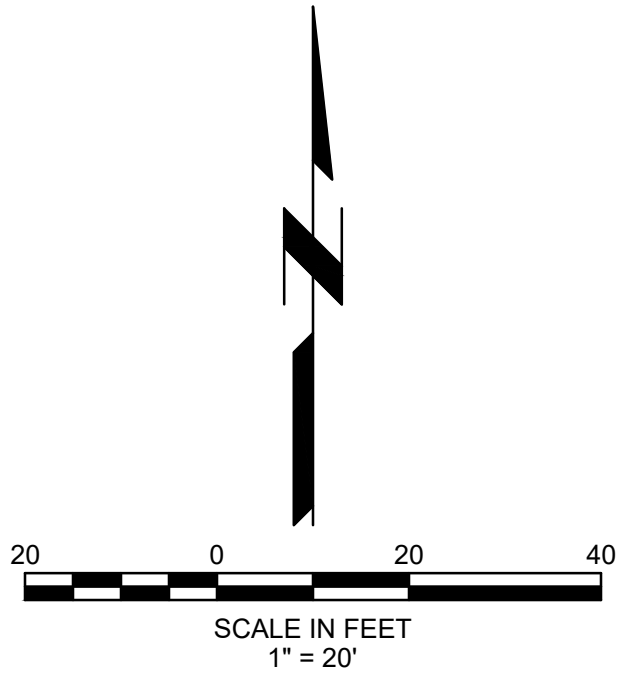

CONSTRUCTION NOTES

- | | |
|---|--|
| 1 | CONSTRUCT GRAVEL PARKING AREA PER DTL 4, DWG CD501. |
| 2 | CONTRACTOR TO INSTALL 3 STEEL POSTS FOR "GARNET HILL RECREATION AREA" SIGN PER DTL 5, DWG CD504 . SIGN TO BE INSTALLED BY BLM. |
| 3 | CONTRACTOR TO INSTALL 2 STEEL POSTS FOR "KEYSTONE JUNCTION" SIGN PER DTL 4, DWG CD504. SIGN TO BE INSTALLED BY BLM. |
| 4 | INSTALL ROCKART KIOSK 03-420 OR APPROVED EQUIVALENT. REFER TO DTL 2, DWG CD502. |

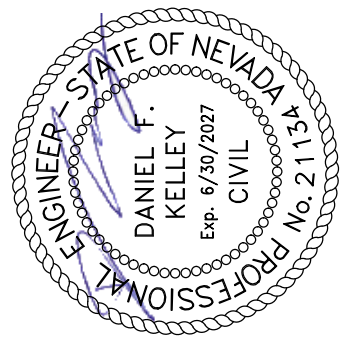

UNITED STATES DEPARTMENT OF THE INTERIOR
BUREAU OF LAND MANAGEMENT

GARNET HILL RECREATION AREA TITLE I AND II SERVICES

BUREAU OF LAND MANAGEMENT DISTRICT OFFICE
ELY, NEVADA


Project Status	Issue Date
100% CONSTRUCTION DOCUMENTS	12/16/2025
BLM Project #	140L0621D0006
Drawn By	ABROWN
Checked By	D.KELLEY

Revision Issue	Date
Description	
Rev. #	

03 - KEYSTONE JUNCTION
KEYSTONE SITE PLAN


3CS-101

19 Dec 2025

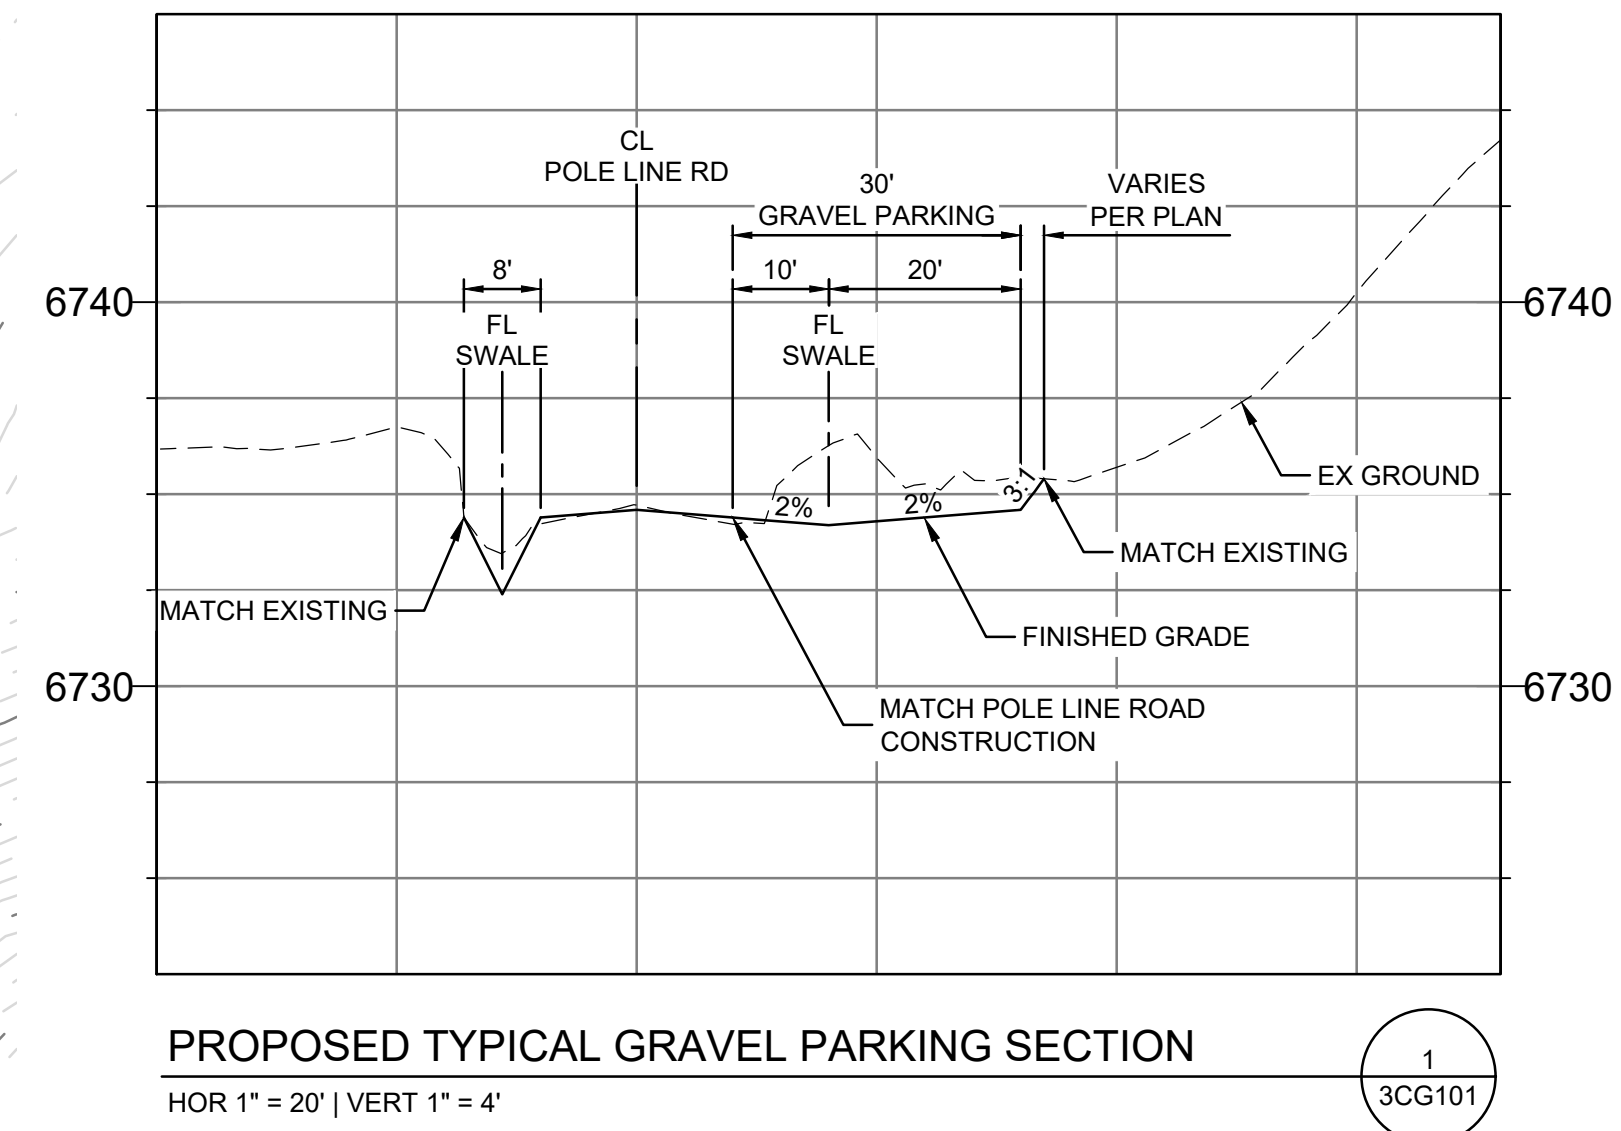


CUT/FILL VOLUMES	
CUT:	90 CY
FILL:	11 CY
NET:	79 CY (CUT)



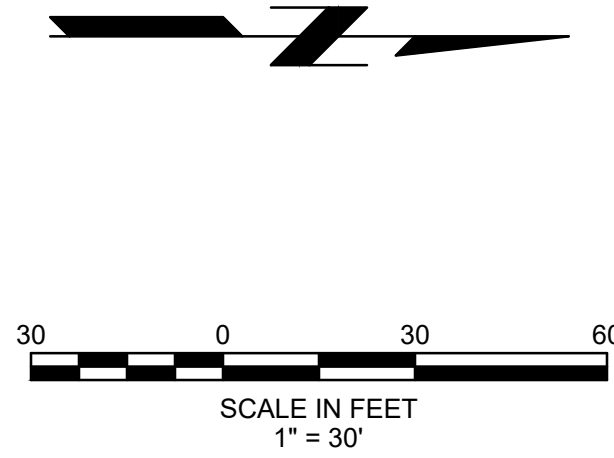

①	REMOVE EXISTING VEGETATION. VEGETATION REMOVAL TO BE LIMITED AS MUCH AS PRACTICAL TO MAINTAIN CAMPSITE PRIVACY
②	ABANDON EXISTING DIRT ROAD IN PLACE

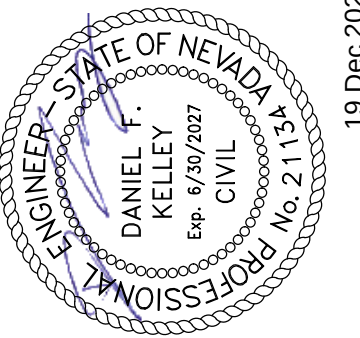

0707 333 67

UNITED STATES DEPARTMENT OF THE INTERIOR
BUREAU OF LAND MANAGEMENT

BUREAU OF LAND MANAGEMENT DISTRICT OFFICE
ELY, NEVADA

Project Status	Issue Date
100%	12/16/2025
CONSTRUCTION	
DOCUMENTS	
BLM Project #	140L0621D0006
Drawn By	A.BROWN
Checked By	D.KELLEY

Rev. #	Description	Date
--------	-------------	------

04 - GARNET HILL LOWER LOWER CAMPGROUND DEMOLITION PLAN


4CR101



 $1'' = 20'$

1
4CR101

P:\Projects\BLM - NV & CA ID\Task Orders\Task 27 - Garnet Hill Recreation Area\Task 27 - Garnet Hill Lower Campground\Drawings\04 - GARNET HILL LOWER CAMPGROUND\04-03-04-CS.dwg, 12/16/2025 8:16 AM KHALVESTUTO

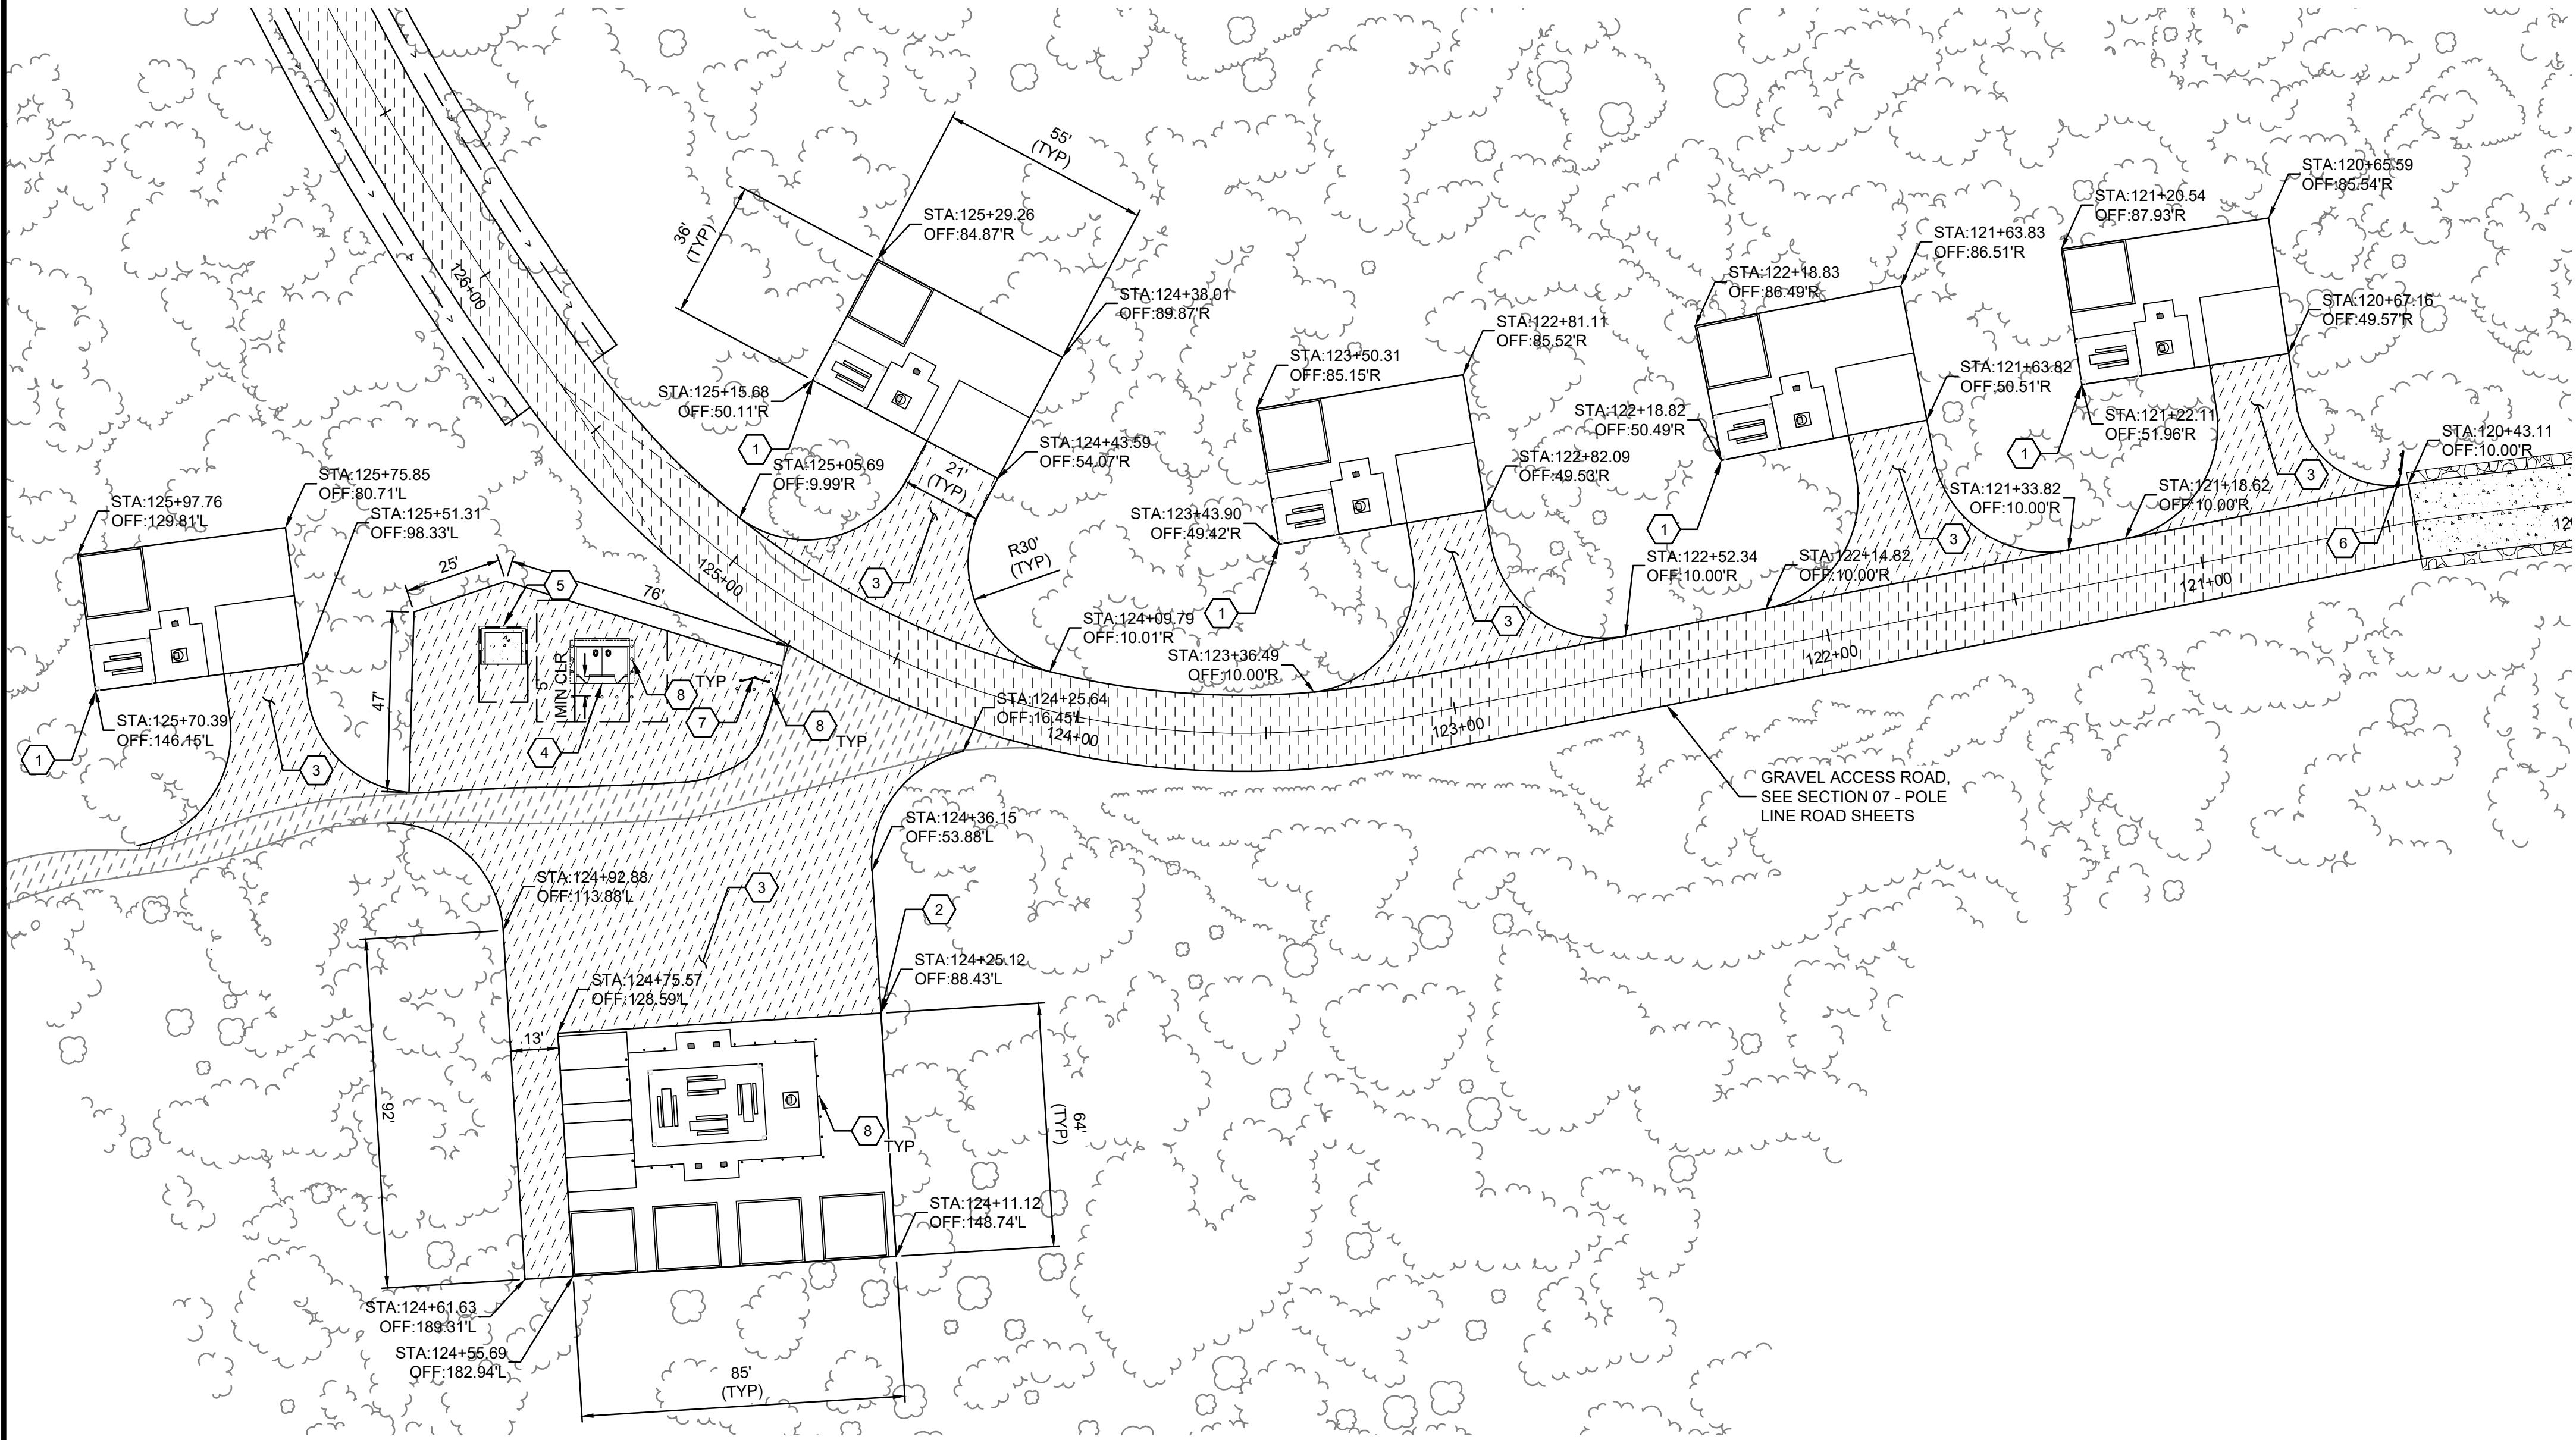

LOWER CAMPGROUND SITE PLAN


1
4CS101



30 0 30 60
SCALE IN FEET
1" = 30'

CONSTRUCTION NOTES

1	CONSTRUCT 55'x36' INDIVIDUAL CAMPSITE PER DTL 1, DWG CD503.
2	CONSTRUCT 85'x64' GROUP CAMPSITE PER DTL 2, DWG CD503.
3	CONSTRUCT GRAVEL ROAD PER DTL 4, DWG CD501.
4	CONSTRUCT DOUBLE VAULT TOILET PER DTL 1, DWG CD502.
5	CONSTRUCT TRASH ENCLOSURE PER DTL 2, DWG CD505.
6	CONTRACTOR TO INSTALL 2 STEEL POSTS FOR "GARNET HILL LOWER CAMPGROUND" SIGN PER DTL 4, DWG CD504. SIGN TO BE INSTALLED BY BLM.
7	INSTALL ROCKART KIOSK 03-441 OR APPROVED EQUIVALENT. REFER TO DTL 2, DWG CD502.
8	INSTALL VEHICLE PROTECTION BOLLARDS WITH ADA COMPLIANCE PER DTL 6, DWG CD501.

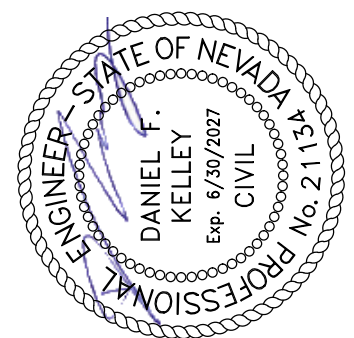

UNITED STATES DEPARTMENT OF THE INTERIOR
BUREAU OF LAND MANAGEMENT

GARNET HILL RECREATION AREA TITLE I
AND II SERVICES





BUREAU OF LAND MANAGEMENT DISTRICT OFFICE
ELY, NEVADA

Revision Issue	Rev. #	Description	Date	Project Status	Issue Date
100% CONSTRUCTION DOCUMENTS	1	BLM Project # 140L0621D0006	12/16/2025	Drawn By A.BROWN Checked By D.KELLEY	12/16/2025

04 - GARNET HILL LOWER
LOWER CAMPGROUND SITE PLAN

4CS101



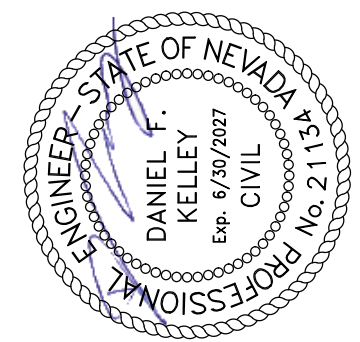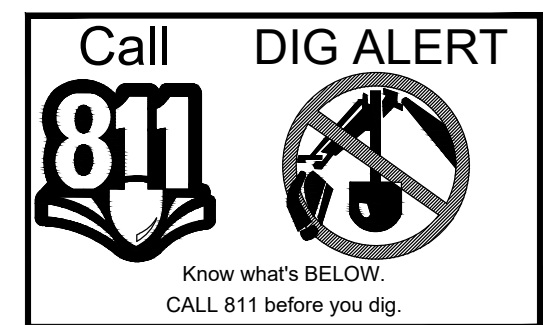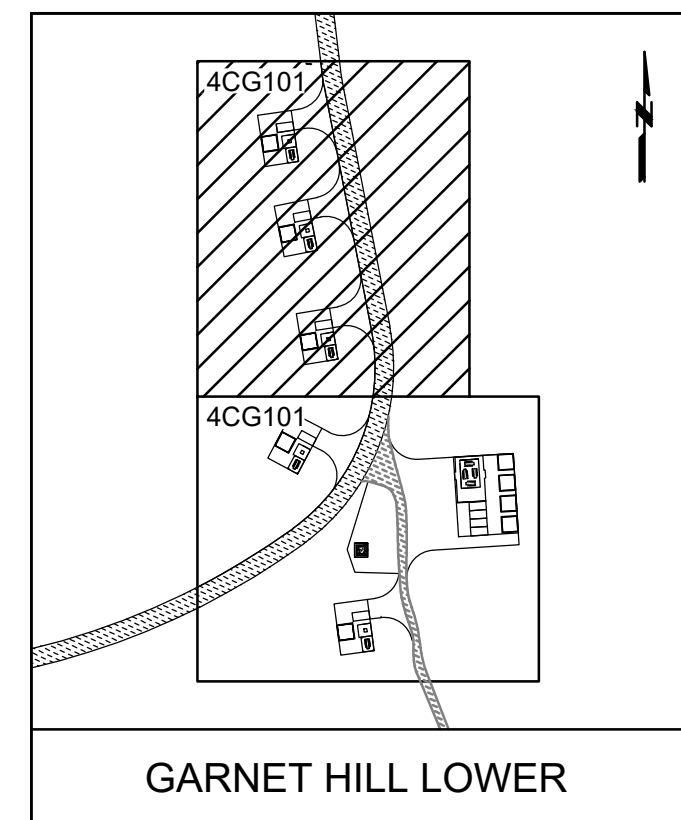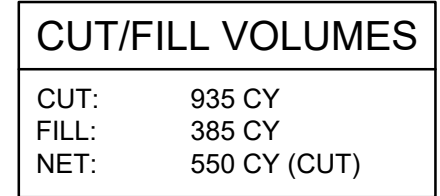

19 Dec 2025

UNITED STATES DEPARTMENT OF THE INTERIOR
BUREAU OF LAND MANAGEMENT


**GARNET HILL RECREATION AREA TITLE I
AND II SERVICES**

BUREAU OF LAND MANAGEMENT DISTRICT OFFICE
ELY, NEVADA

Rev. #	Revision Issue Description	Date	Project Status	Issue Date
			100% CONSTRUCTION DOCUMENTS	12/16/2025
			BLM Project #	140L0621D0006
			Drawn By	A. BROWN
			Checked By	D. KELLEY


04 - GARNET HILL LOWER
LOWER CAMPGROUND GRADING
PLAN

4CG101

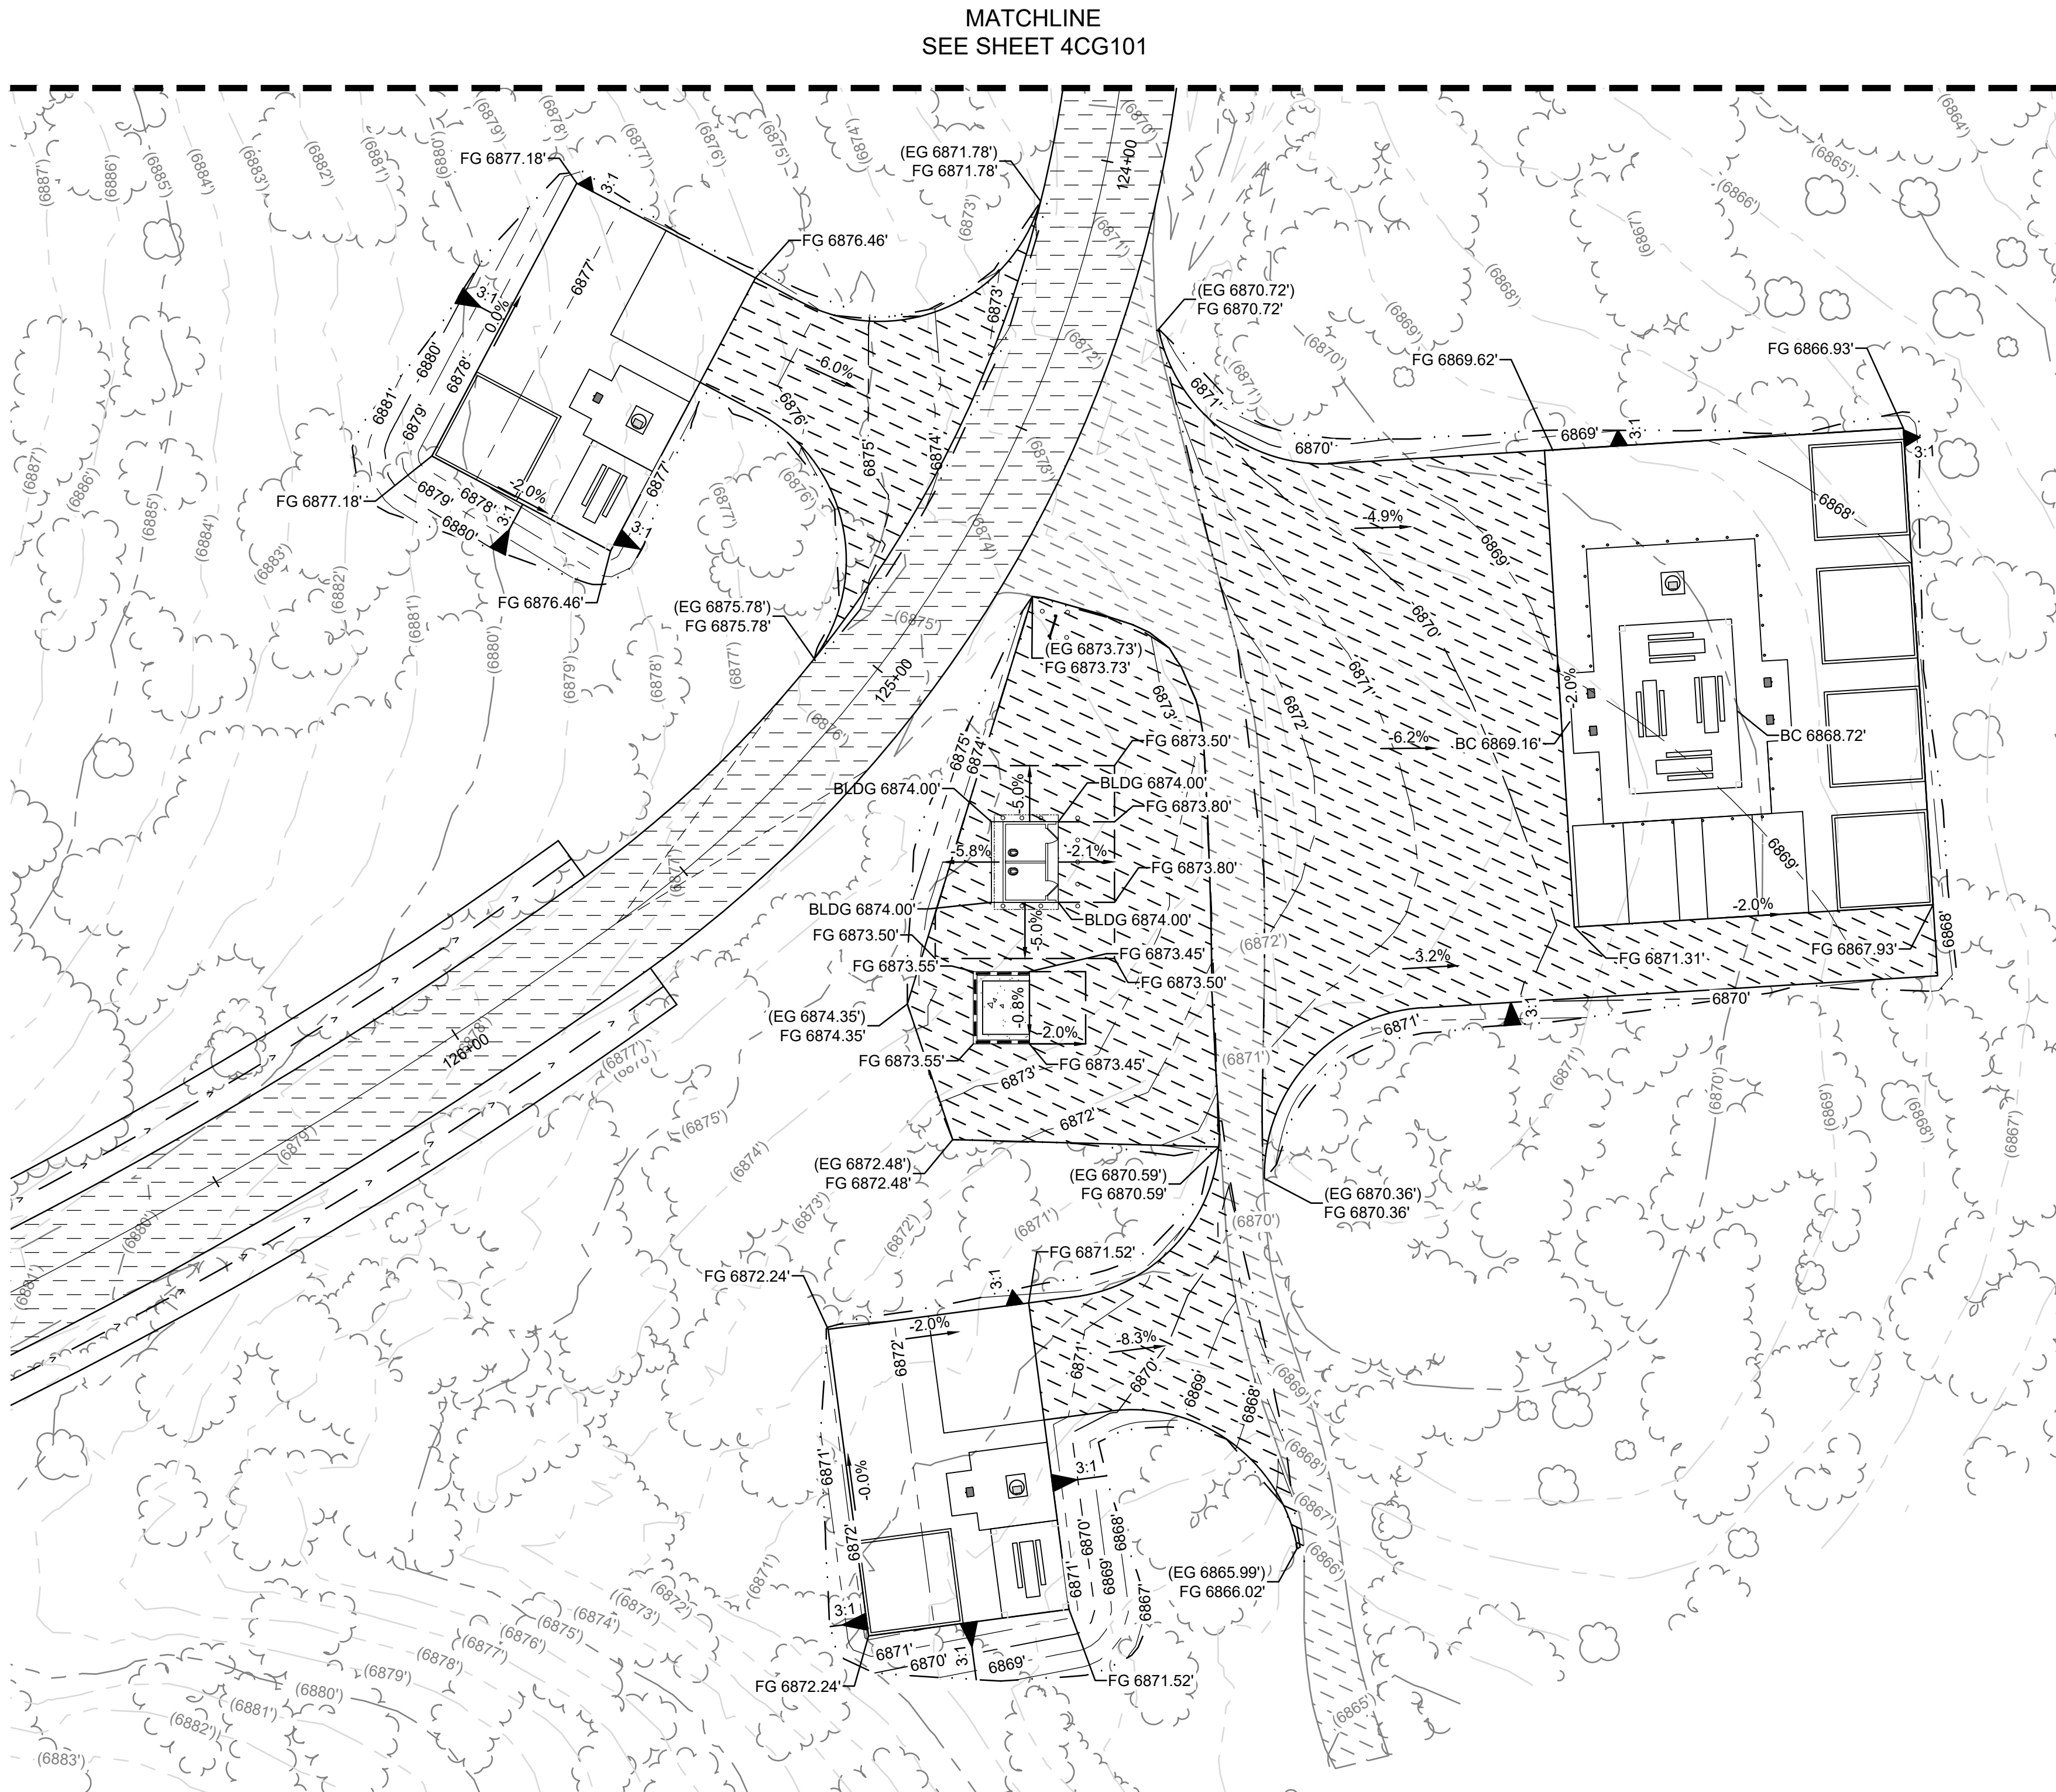


1" = 20'

1
4CG102

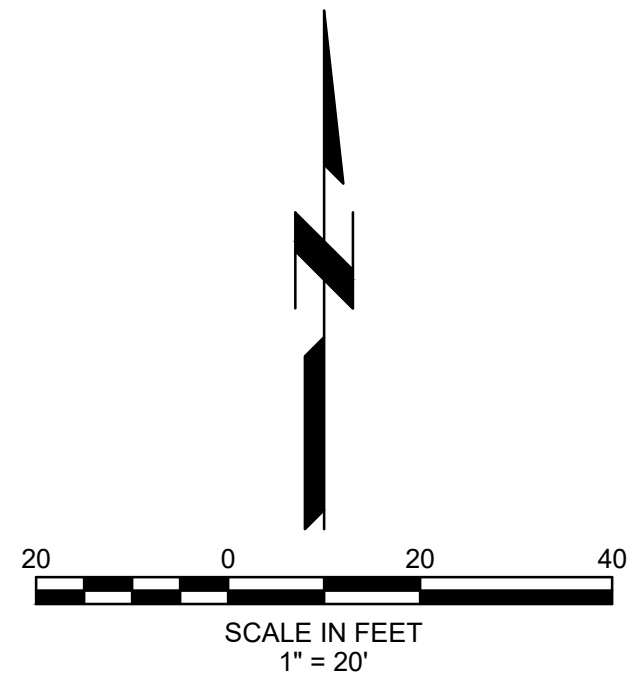

CUT/FILL VOLUMES	
CUT:	935 CY
FILL:	385 CY
NET:	550 CY (CUT)

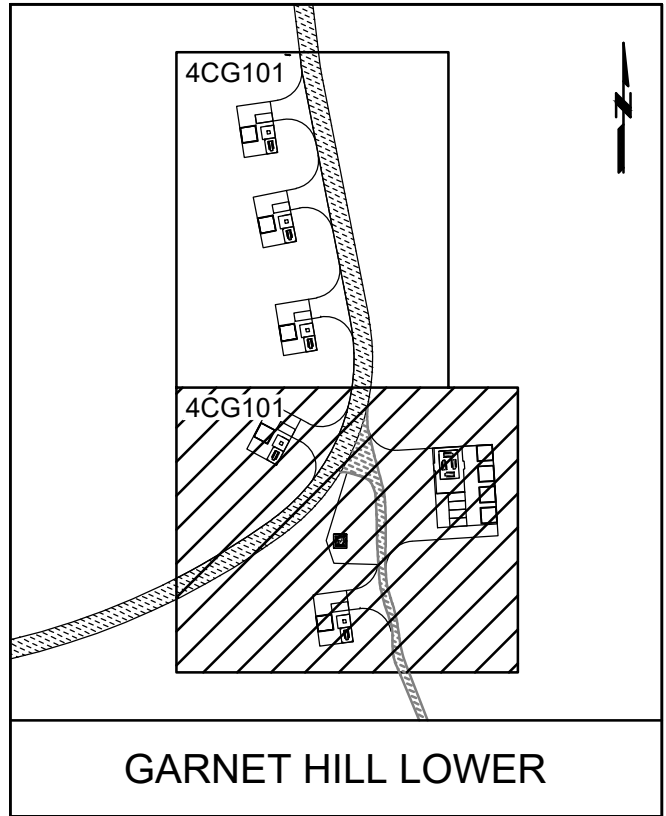

UNITED STATES DEPARTMENT OF THE INTERIOR
BUREAU OF LAND MANAGEMENT

**GARNET HILL RECREATION AREA TITLE I
AND II SERVICES**

BUREAU OF LAND MANAGEMENT DISTRICT OFFICE
ELY, NEVADA

Project Status
100%
CONSTRUCTION
DOCUMENTS

Issue Date
12/16/2025

Rev. #

Revision Issue
Description

Date

BLM Project #
140L0621D0006



Drawn By
A.BROWN

Checked By
D.KELLEY


04 - GARNET HILL LOWER
LOWER CAMPGROUND GRADING
PLAN

4CG102

1" = 30'

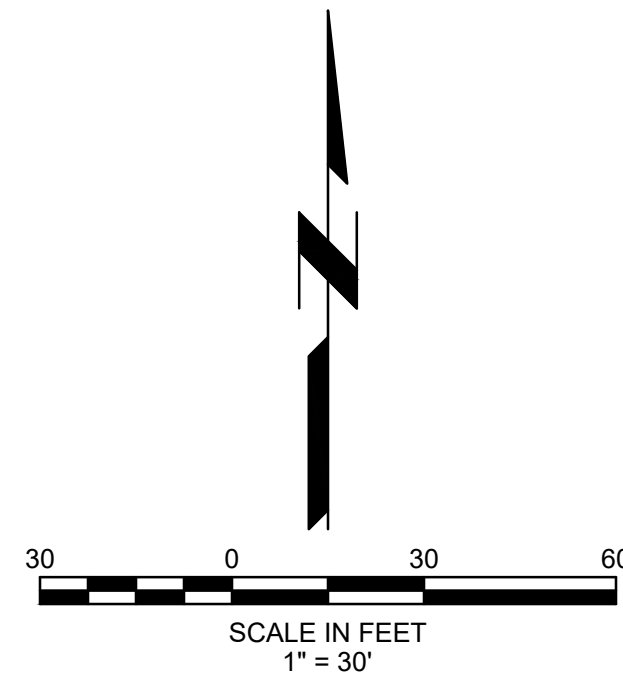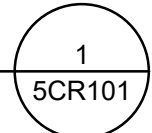

DEMOLITION NOTES	
①	REMOVE EXISTING VEGETATION. VEGETATION REMOVAL TO BE LIMITED AS MUCH AS PRACTICAL TO MAINTAIN CAMPSITE PRIVACY
②	ABANDON EXISTING DIRT ROAD IN PLACE

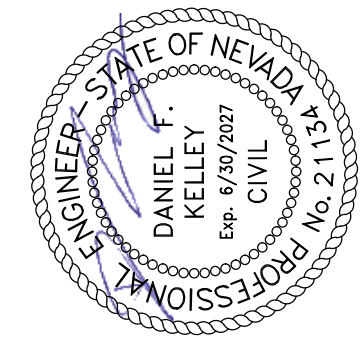

19 Dec 2025




BUREAU OF LAND MANAGEMENT DISTRICT OFFICE
ELY, NEVADA

Rev. #	Revision Issue Description	Date	Project Status	Issue Date
			100% CONSTRUCTION DOCUMENTS	12/16/2025
			BLM Project #	140L0621D0006
			Drawn By	A BROWN
			Checked By	D KELLEY


5CR101

P:\Projects\BLM - NV & CA\IDOTask Orders\Task 27 - Garnet Hill Recreation Area Title I & II Services\Engineering\Drawings\Production\Drawings\05 - GARNET HILL UPPER CAMPGROUND\2025-003-05-CS.dwg 12/16/2025 8:14 AM KVALVESTUTO

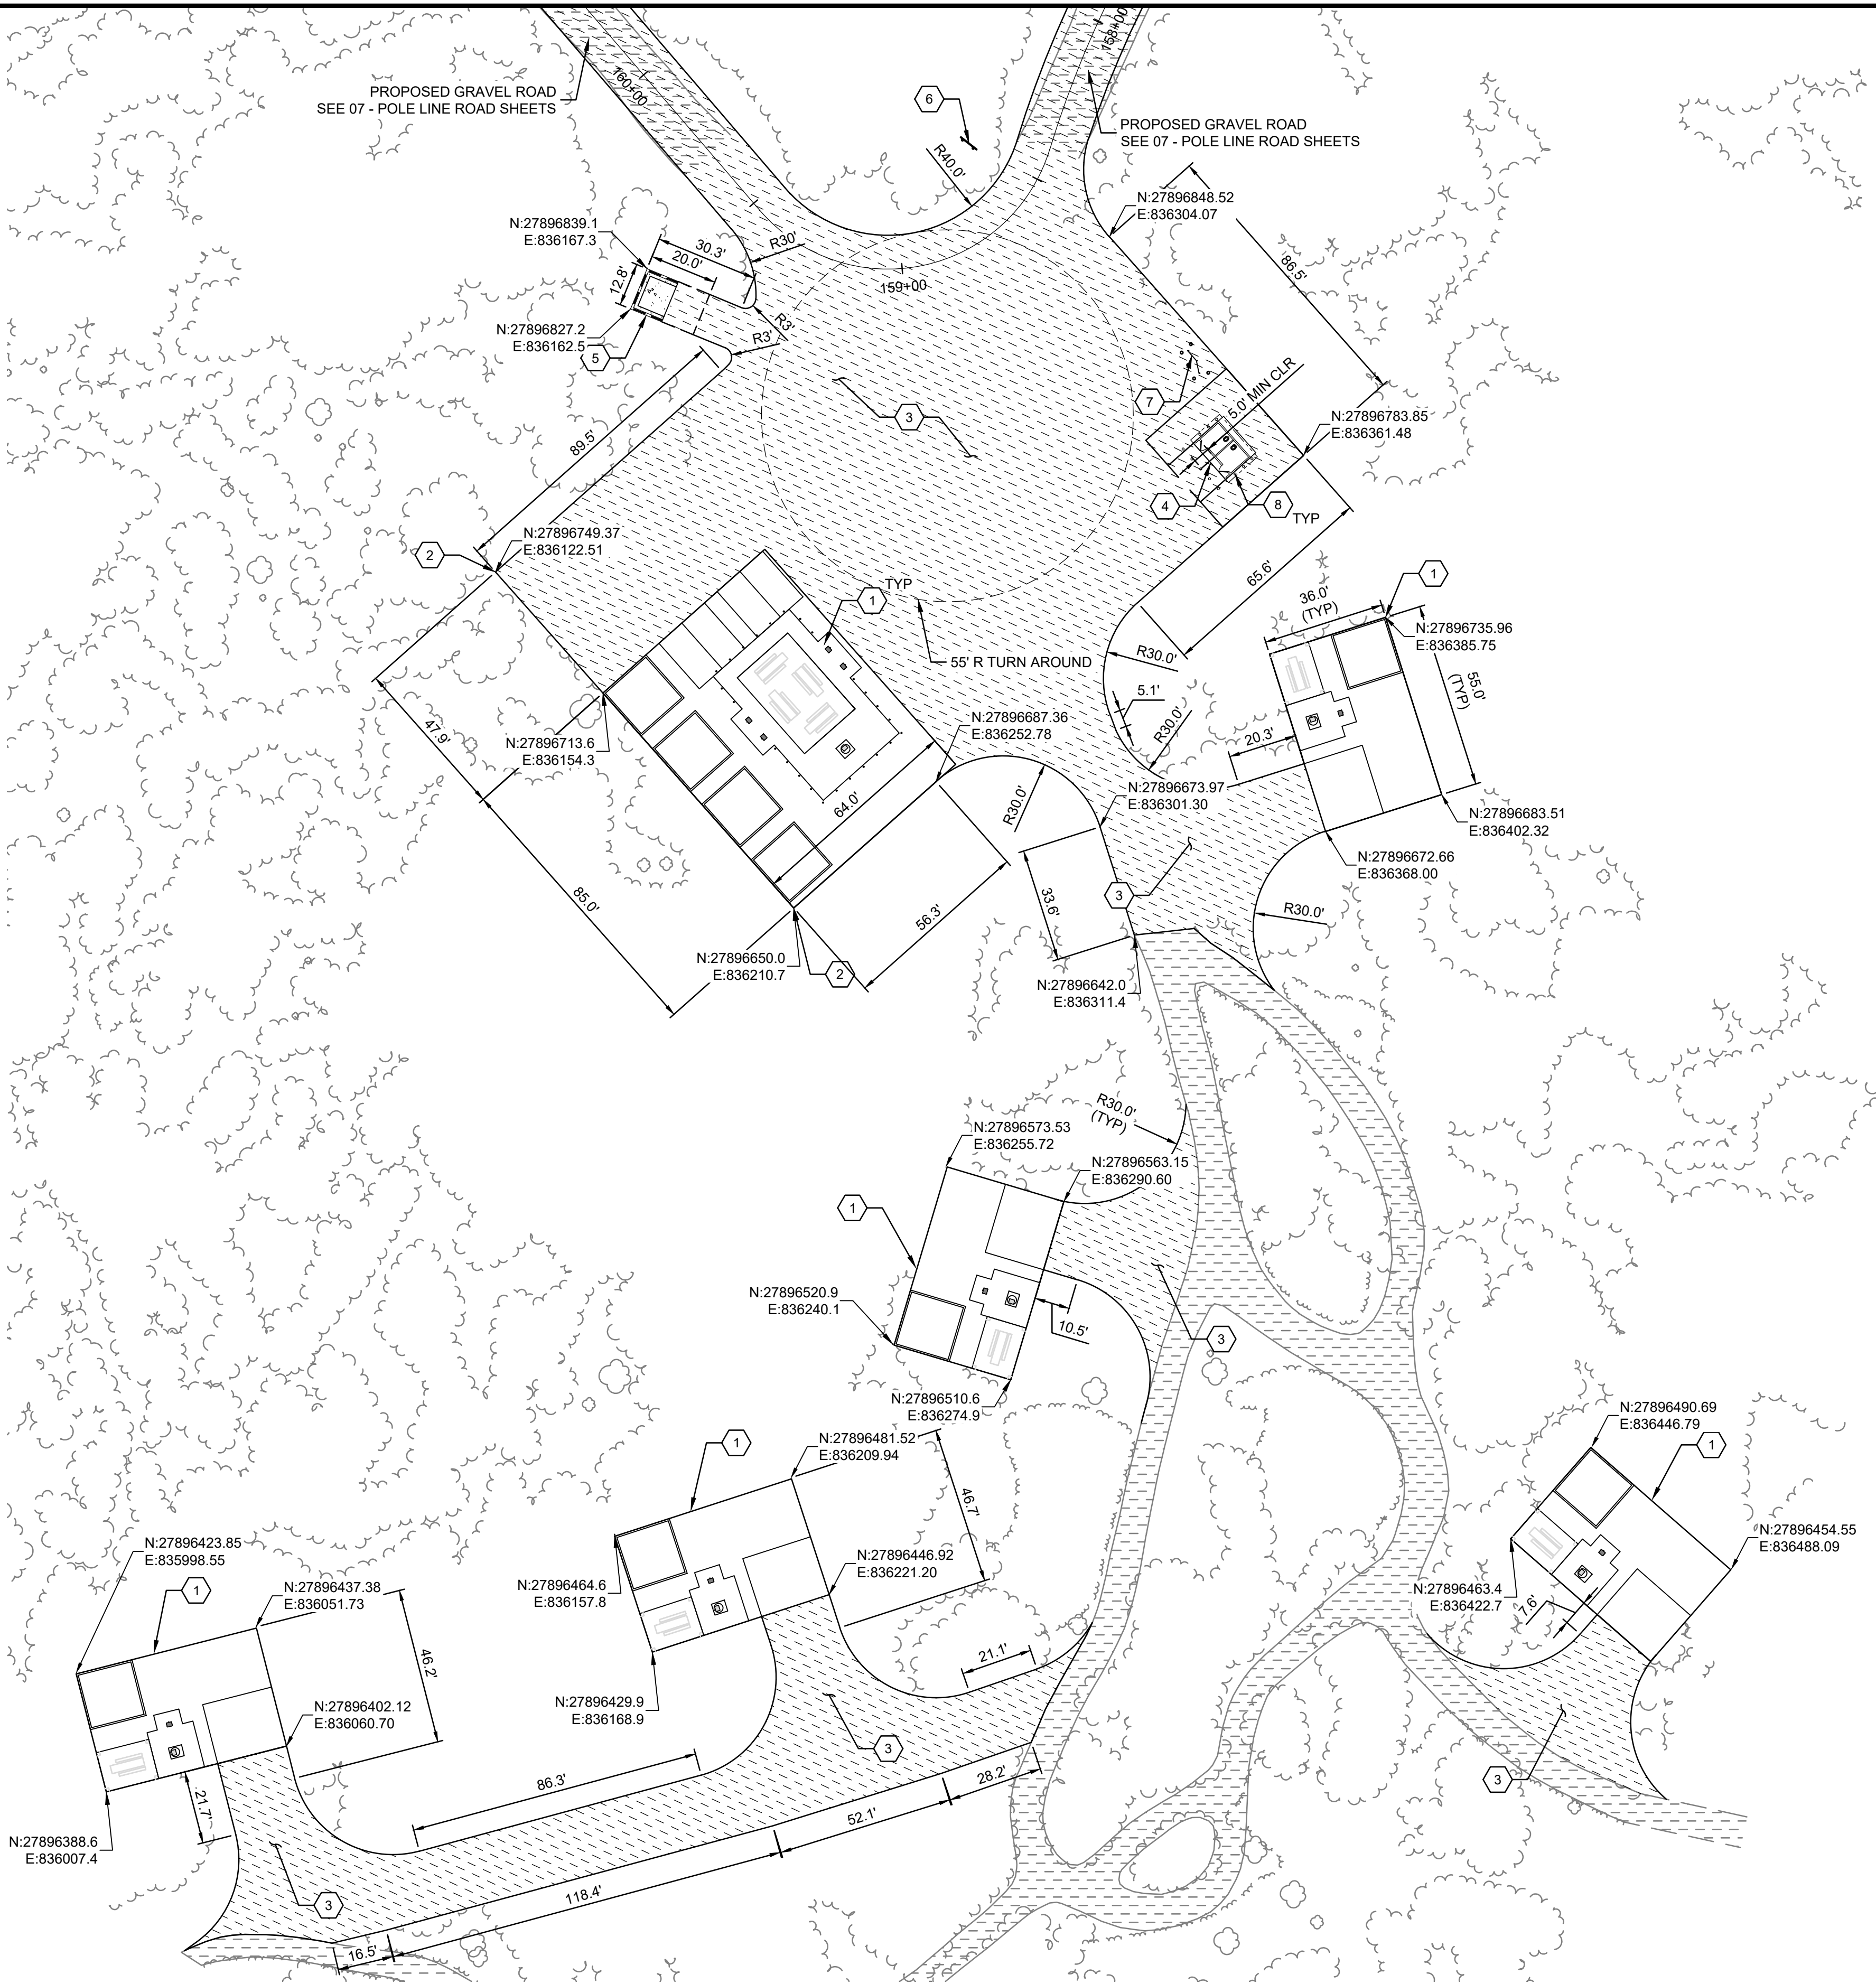


UPPER CAMPGROUND SITE PLAN
1" = 30'

1
5CS101

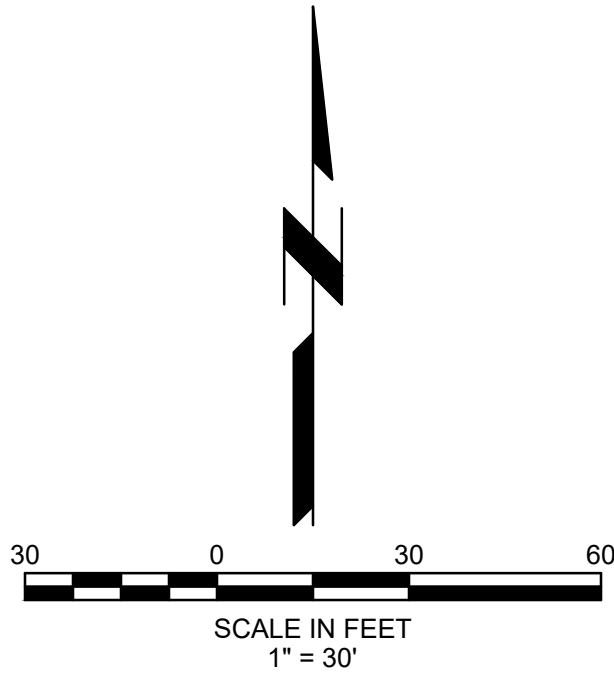

CONSTRUCTION NOTES

1	CONSTRUCT 55'x36' INDIVIDUAL CAMPSITE PER DTL 1, DWG CD503.
2	CONSTRUCT 85'x64' GROUP CAMPSITE PER DTL 2, DWG CD503.
3	CONSTRUCT GRAVEL ROAD PER DTL 4, DWG CD501.
4	CONSTRUCT DOUBLE VAULT TOILET PER DTL 1, DWG CD502.
5	CONSTRUCT TRASH ENCLOSURE PER DTL 2, DWG CD505.
6	CONTRACTOR TO INSTALL 2 STEEL POSTS FOR "GARNET HILL UPPER CAMPGROUND" SIGN PER DTL 4, DWG CD504. SIGN TO BE INSTALLED BY BLM.
7	INSTALL ROCKART KIOSK 03-441 OR APPROVED EQUIVALENT. REFER TO DTL 2, DWG CD502.
8	INSTALL VEHICLE PROTECTION BOLLARDS WITH ADA COMPLIANCE PER DTL 6, DWG CD501.

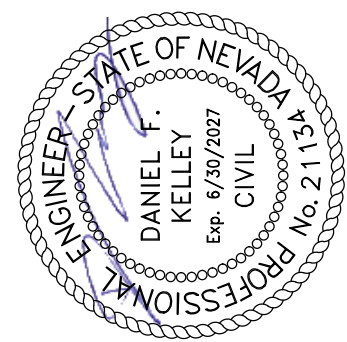

19 Dec 2025

UNITED STATES DEPARTMENT OF THE INTERIOR
BUREAU OF LAND MANAGEMENT

GARNET HILL RECREATION AREA TITLE I
AND II SERVICES

BUREAU OF LAND MANAGEMENT DISTRICT OFFICE
ELY, NEVADA

Project Status	Issue Date
100% CONSTRUCTION DOCUMENTS	12/16/2025
BLM Project #	140L0621D0006
Drawn By	ABROWN
Checked By	D.KELLEY

Revision Issue	Date
Description	
Rev. #	



05 - GARNET HILL UPPER
UPPER CAMPGROUND SITE PLAN

5CS101

P:\Projects\BLM - NV & CA\IDOTask Orders\Task 27 - Garnet Hill Recreation Area Title I & II Services\Engineering\Drawings\Production\Drawings\05 - GARNET HILL UPPER CAMPGROUND\2025-003-05-CG.dwg, 12/16/2025 8:15 AM ABRONW




CUT/FILL VOLUMES	
CUT:	1160 CY
FILL:	3680 CY
NET:	2520 CY (CUT)

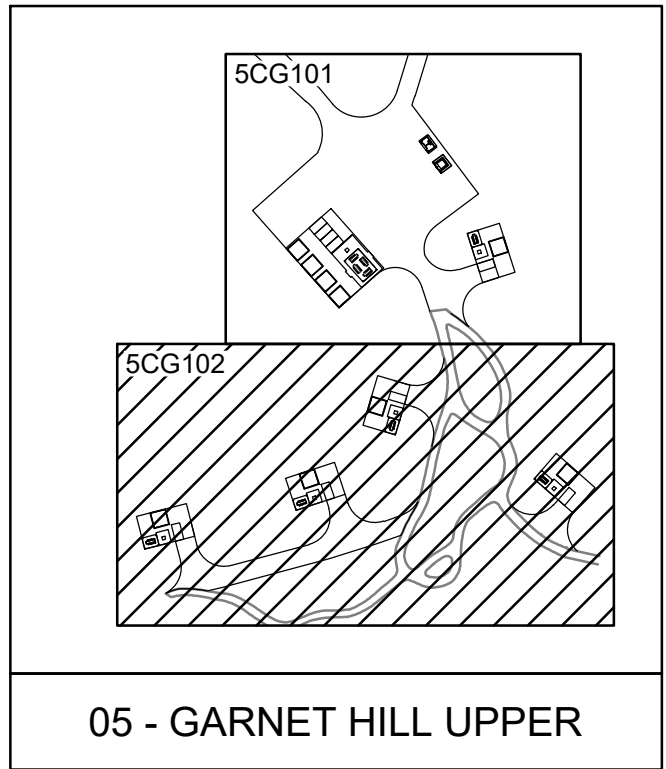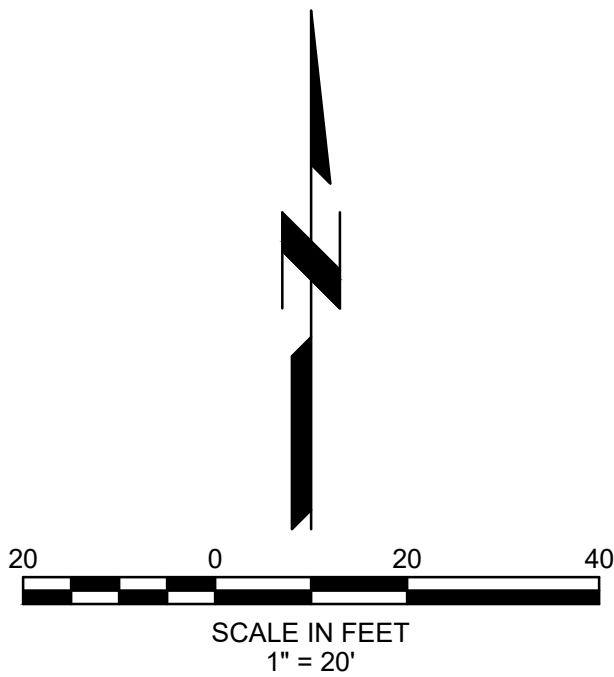

UPPER CAMPGROUND GRADING PLAN
1" = 20'

1
5CG102

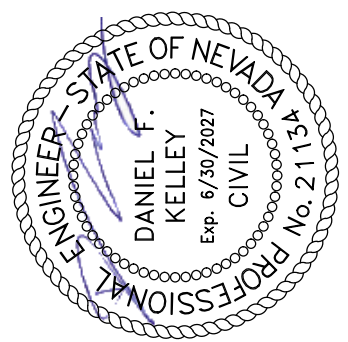

19 Dec 2025

UNITED STATES DEPARTMENT OF THE INTERIOR
BUREAU OF LAND MANAGEMENT

GARNET HILL RECREATION AREA TITLE I AND II SERVICES

BUREAU OF LAND MANAGEMENT DISTRICT OFFICE
ELY, NEVADA


Project Status	Issue Date
100% CONSTRUCTION DOCUMENTS	12/16/2025
BLM Project #	140L0621D0006
Drawn By	ABRONW
Checked By	D.KELLEY

Revision Issue	Date
Description	
Rev. #	

05 - GARNET HILL UPPER
UPPER CAMPGROUND GRADING
PLAN


5CG102

P:\Projects\BLM - NV & CA IDIO\Task Orders\Task 27 - Garnet Hill Recreation Area Title I & II Services\Engineering\Drawings\Production Drawings\06 - GARNET HILL MAIN TRAIL HEAD\06-003-CR.dwg 12/19/2025 8:14 AM KMA\VESTUTO

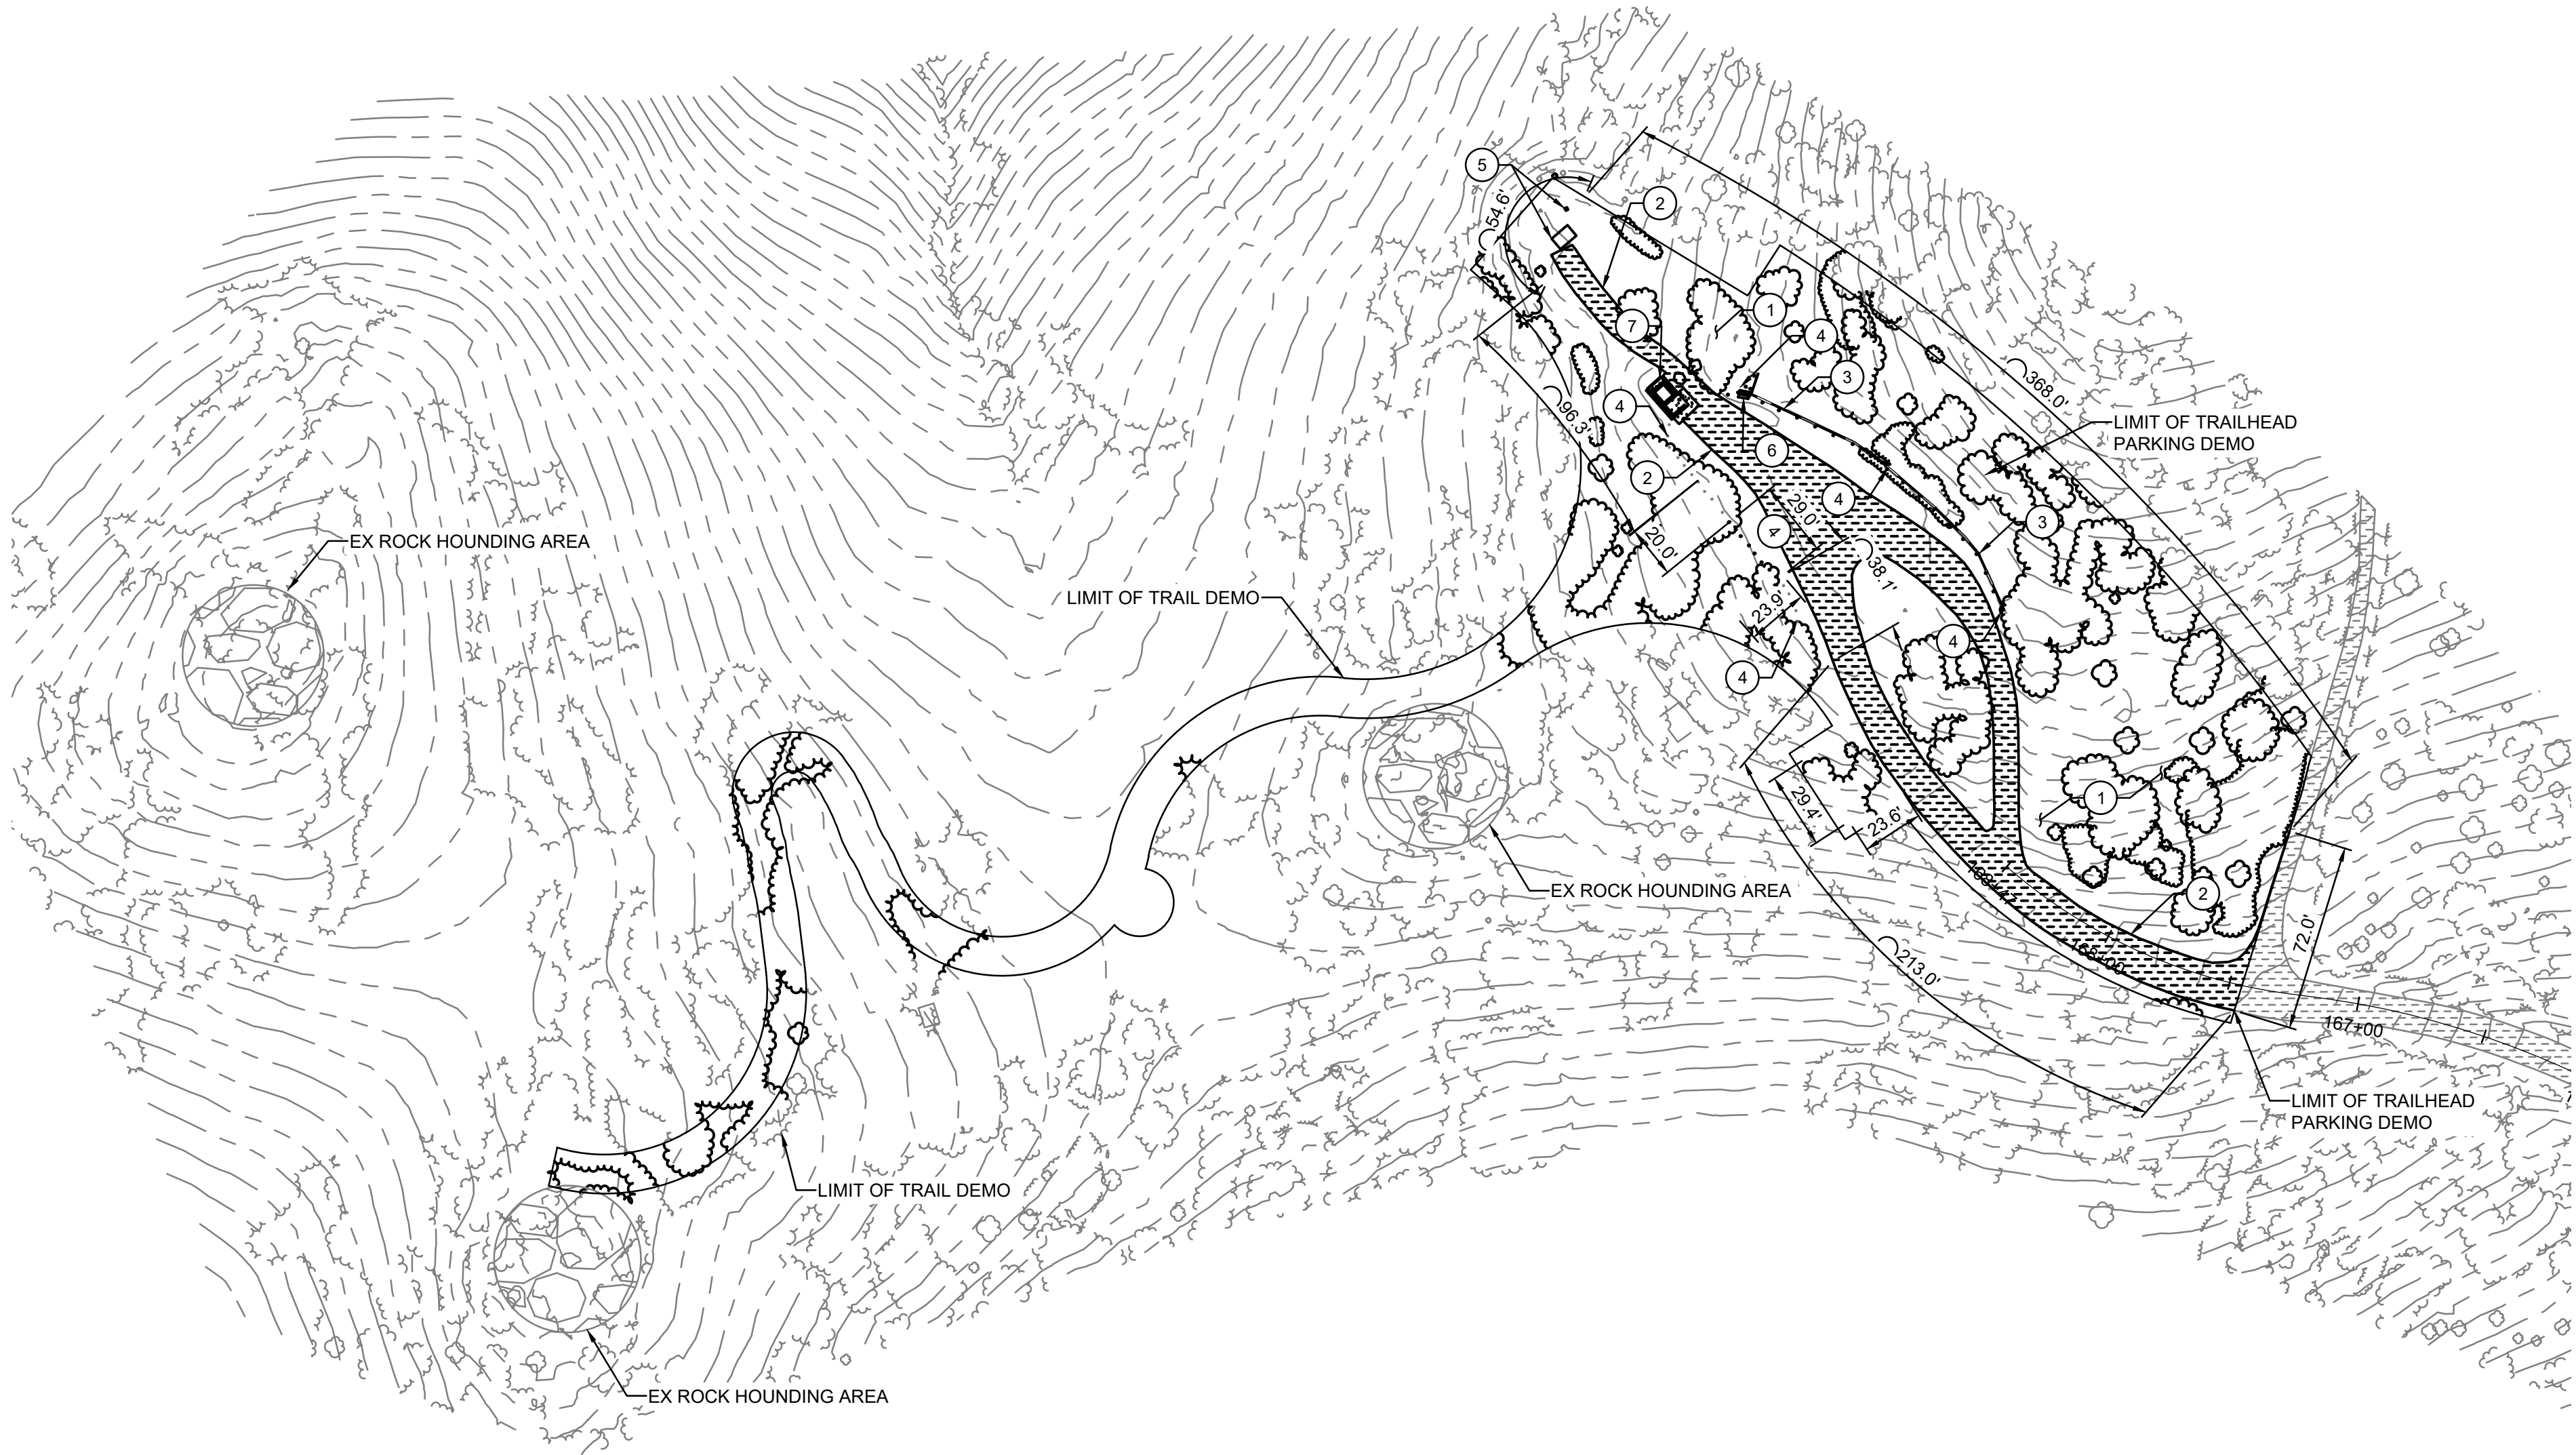


OVERALL MAIN TRAILHEAD
1" = 50'

1
6CR101

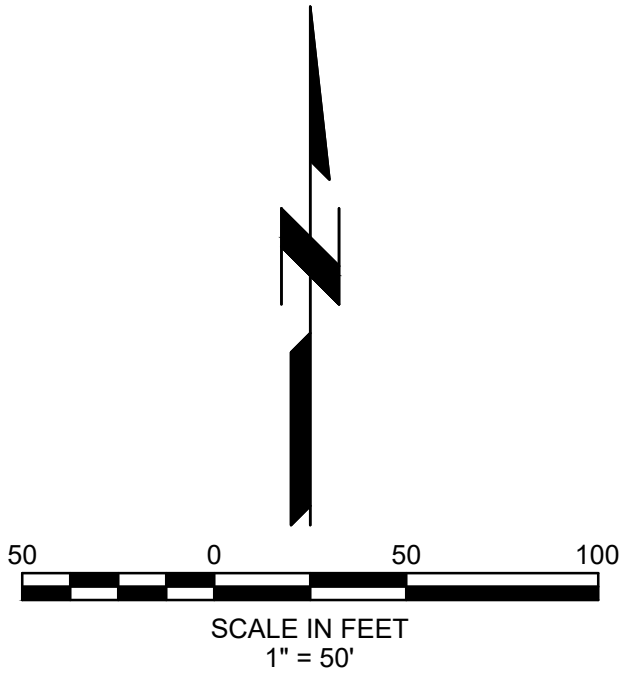

DEMOLITION NOTES	
①	CLEAR AND GRUB EXISTING VEGETATION
②	ABANDON EXISTING DIRT ROAD IN PLACE
③	DEMOLISH EXISTING RETAINING WALL
④	REMOVE EXISTING (47) STEEL POST BOLLARDS. CONTRACTOR SHALL DETERMINE IF THEY CAN BE REUSED. IF NOT REUSED, RETURN TO BLM.
⑤	REMOVE EXISTING PICNIC TABLE AND BBQ
⑥	DEMOLISH EXISTING WOODEN STAIRS
⑦	DEMOLISH EXISTING VAULT TOILET PER NDEP STANDARDS. DISPOSE OF OFF-SITE.

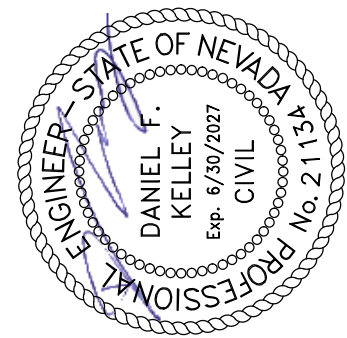

UNITED STATES DEPARTMENT OF THE INTERIOR
BUREAU OF LAND MANAGEMENT

**GARNET HILL RECREATION AREA TITLE I
AND II SERVICES**

BUREAU OF LAND MANAGEMENT DISTRICT OFFICE
ELY, NEVADA

Project Status
100% CONSTRUCTION DOCUMENTS
BLM Project #
Drawn By
Checked By

Issue Date
12/16/2025
140L0621D0006
A.BROWN
D.KELLEY


Revision Issue
Description
Rev. #

06 - GARNET HILL MAIN TRAIL
MAIN TRAIL DEMOLITION PLAN

6CR101

19 Dec 2025


P:\Projects\BLM - NV & CA\IDOTask Orders\Task 27 - Garnet Hill Recreation Area Title I & II Services\Engineering\Drawings\Production Drawings\06 - GARNET HILL MAIN TRAIL HEAD\06-03-06-CS.dwg, 12/16/2025 8:15 AM ABBROWN

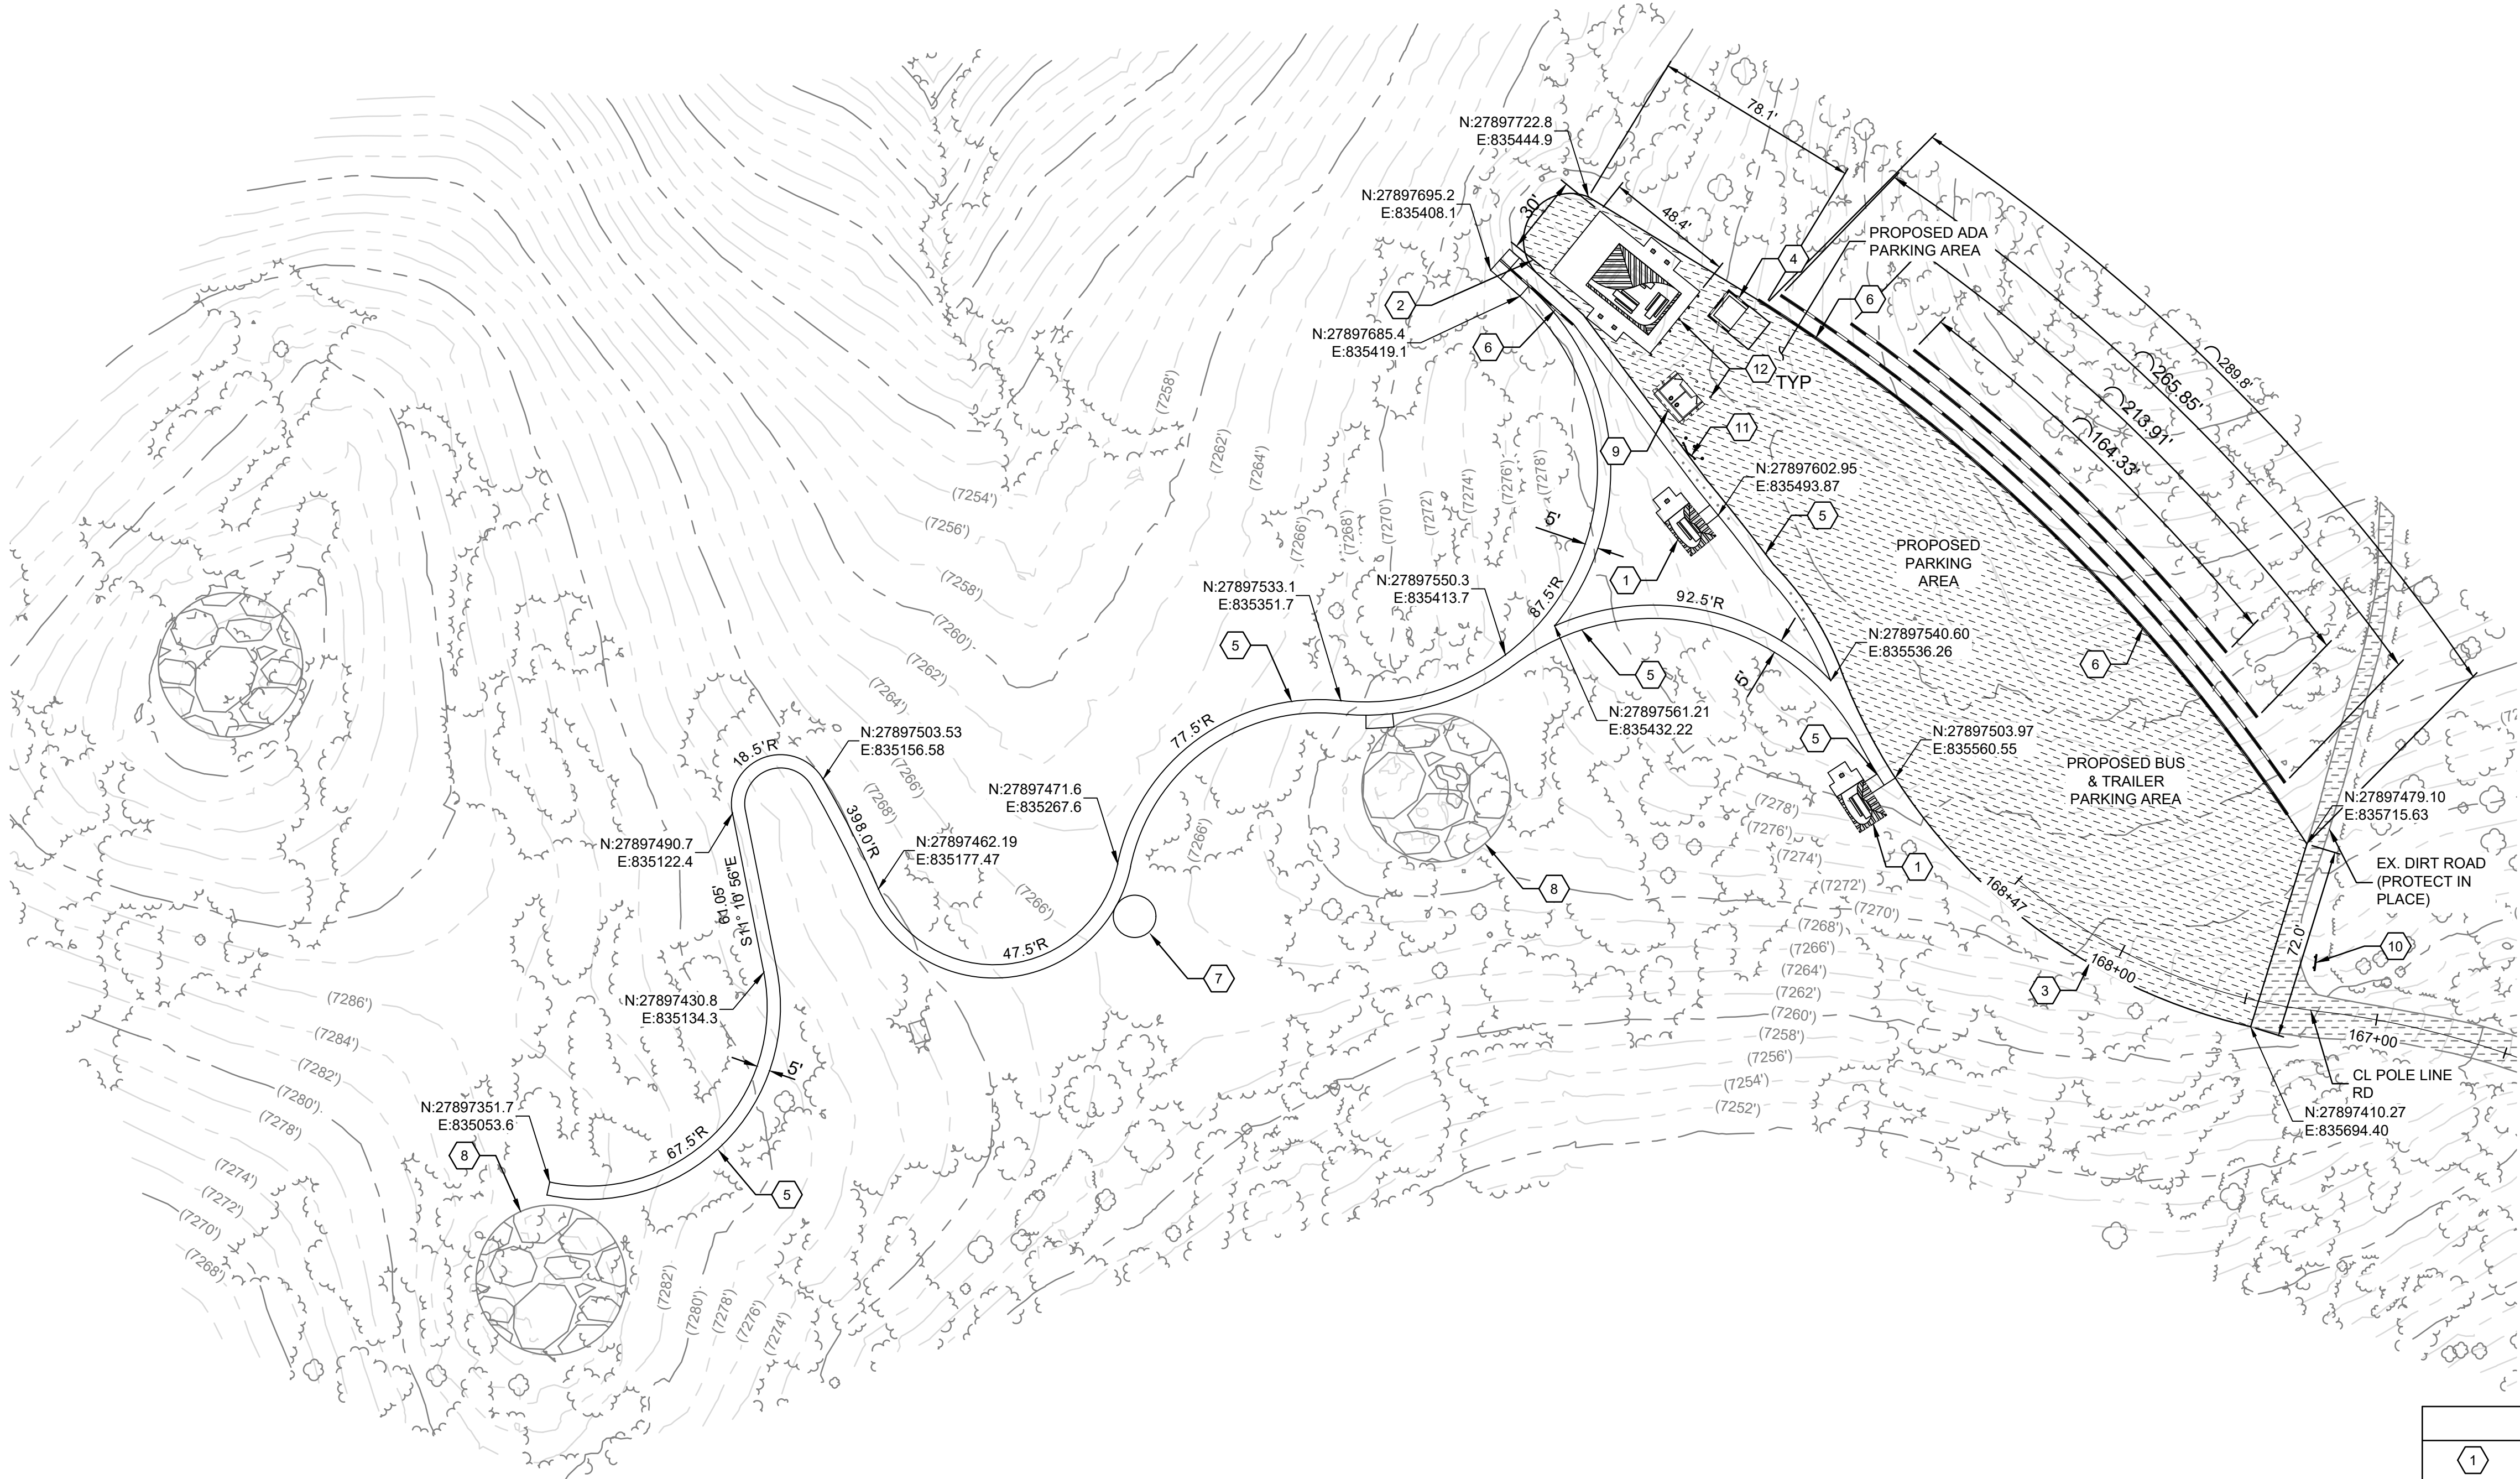

OVERALL MAIN TRAILHEAD
1" = 40'

1
6CS101

CONSTRUCTION NOTES	
1	CONSTRUCT INDIVIDUAL DAY-USE PICNIC SITE PER DTL 4, DWG CD503.
2	CONSTRUCT GROUP DAY-USE PICNIC SITE PER DTL 5, DWG CD503.
3	CONSTRUCT GRAVEL ROAD PER DTL 2, DWG CD504.
4	CONSTRUCT TRASH ENCLOSURE PER DTL 2, DWG CD505.
5	CONSTRUCT ADA COMPLIANT CONCRETE PATH. LONGITUDINAL SLOPE NOT TO EXCEED 5% AND CROSS SLOPE NOT TO EXCEED 2%.
6	CONSTRUCT 4' MAX. MASONRY RETAINING WALLS PER DTL 2, DWG CD501.
7	CONSTRUCT 16" DIAMETER CONCRETE VIEWING AREA. 4" CONCRETE OVER 6" TYPE II AGGREGATE BASE.
8	CONTRACTOR TO COORDINATE WITH BLM ON MEANS AND METHOD FOR REWORKING THE EXISTING ROCK HOUNDING AREAS IN ORDER TO CREATE SMALLER, PUBLIC SAFE SIZED ROCK.
9	CONSTRUCT DOUBLE VAULT TOILET PER DTL 1, DWG CD502.
10	CONTRACTOR TO INSTALL 3 STEEL POSTS FOR "GARNET HILL MAIN TRAILHEAD" SIGN PER DTL 5, DWG CD504. SIGN TO BE INSTALLED BY BLM.
11	INSTALL ROCKART KIOSK 03-441 OR APPROVED EQUIVALENT. REFER TO DTL 2, DWG CD502.
12	INSTALL VEHICLE PROTECTION BOLLARDS WITH ADA COMPLIANCE PER DTL 6, DWG CD501.

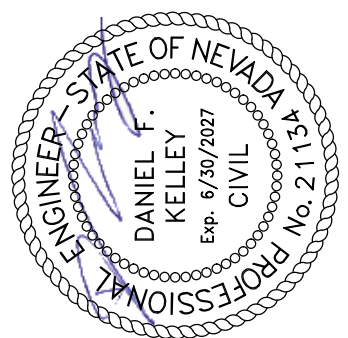

UNITED STATES DEPARTMENT OF THE INTERIOR
BUREAU OF LAND MANAGEMENT

**GARNET HILL RECREATION AREA TITLE I
AND II SERVICES**

BUREAU OF LAND MANAGEMENT DISTRICT OFFICE
ELY, NEVADA

Issue Date
12/16/2025

Project Status
100% CONSTRUCTION DOCUMENTS
BLM Project #
140L0621D0006

Drawn By
ABBROWN

Checked By
D.KELLEY

Revision Issue

Date





Description

Rev. #

06 - GARNET HILL MAIN TRAIL
MAIN TRAIL SITE PLAN

6CS101

19 Dec 2025

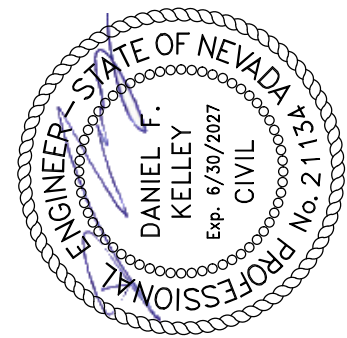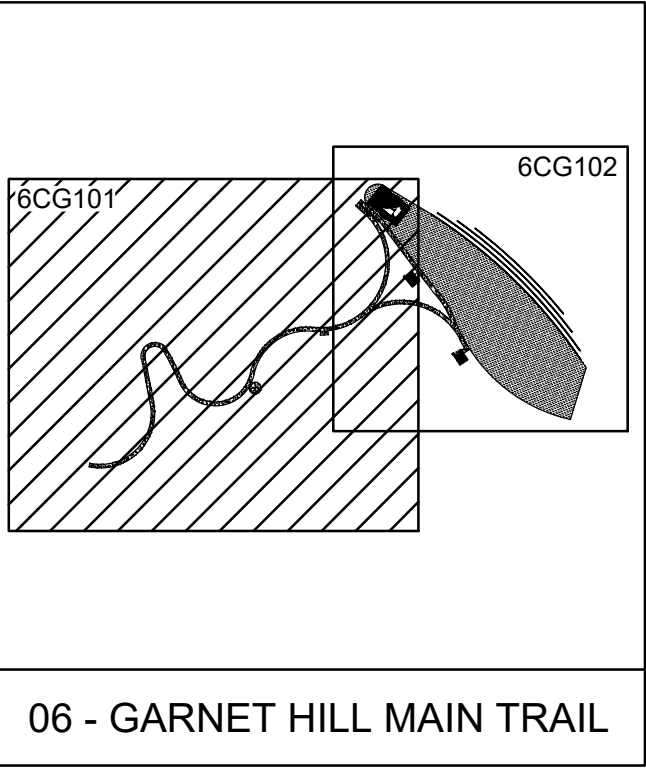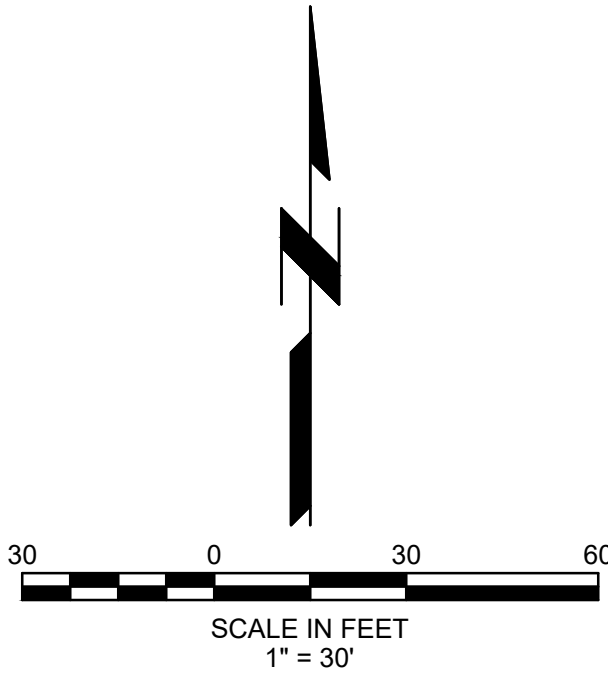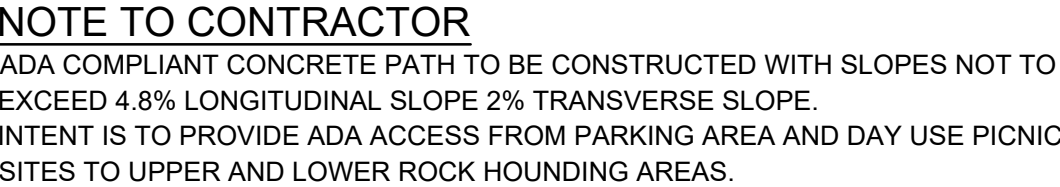

19 Dec 2025

GARNET HILL RECREATION AREA TITLE II AND II SERVICES

BUREAU OF LAND MANAGEMENT DISTRICT OFFICE
ELY, NEVADA


Rev. #	Revision Issue Description	Date	Project Status	Issue Date
			100% CONSTRUCTION DOCUMENTS	12/16/2025
			BLM Project #	140L0621D0006
			Drawn By	A.BROWN
			Checked By	D.KELLEY

06 - GARNET HILL MAIN TRAIL
MAIN TRAIL GRADING PLAN 1

6CG101

P:\Projects\BLM - NV & CA IDIO\Task Orders\Task 27 - Garnet Hill Recreation Area Title I & II Services\Engineering\Drawings\Production Drawings\06 - GARNET HILL MAIN TRAIL HEAD\208-003-06-CG.dwg 12/16/2025 8:15 AM ABBROWN



MATCHLINE
SEE SHEET 6CG101

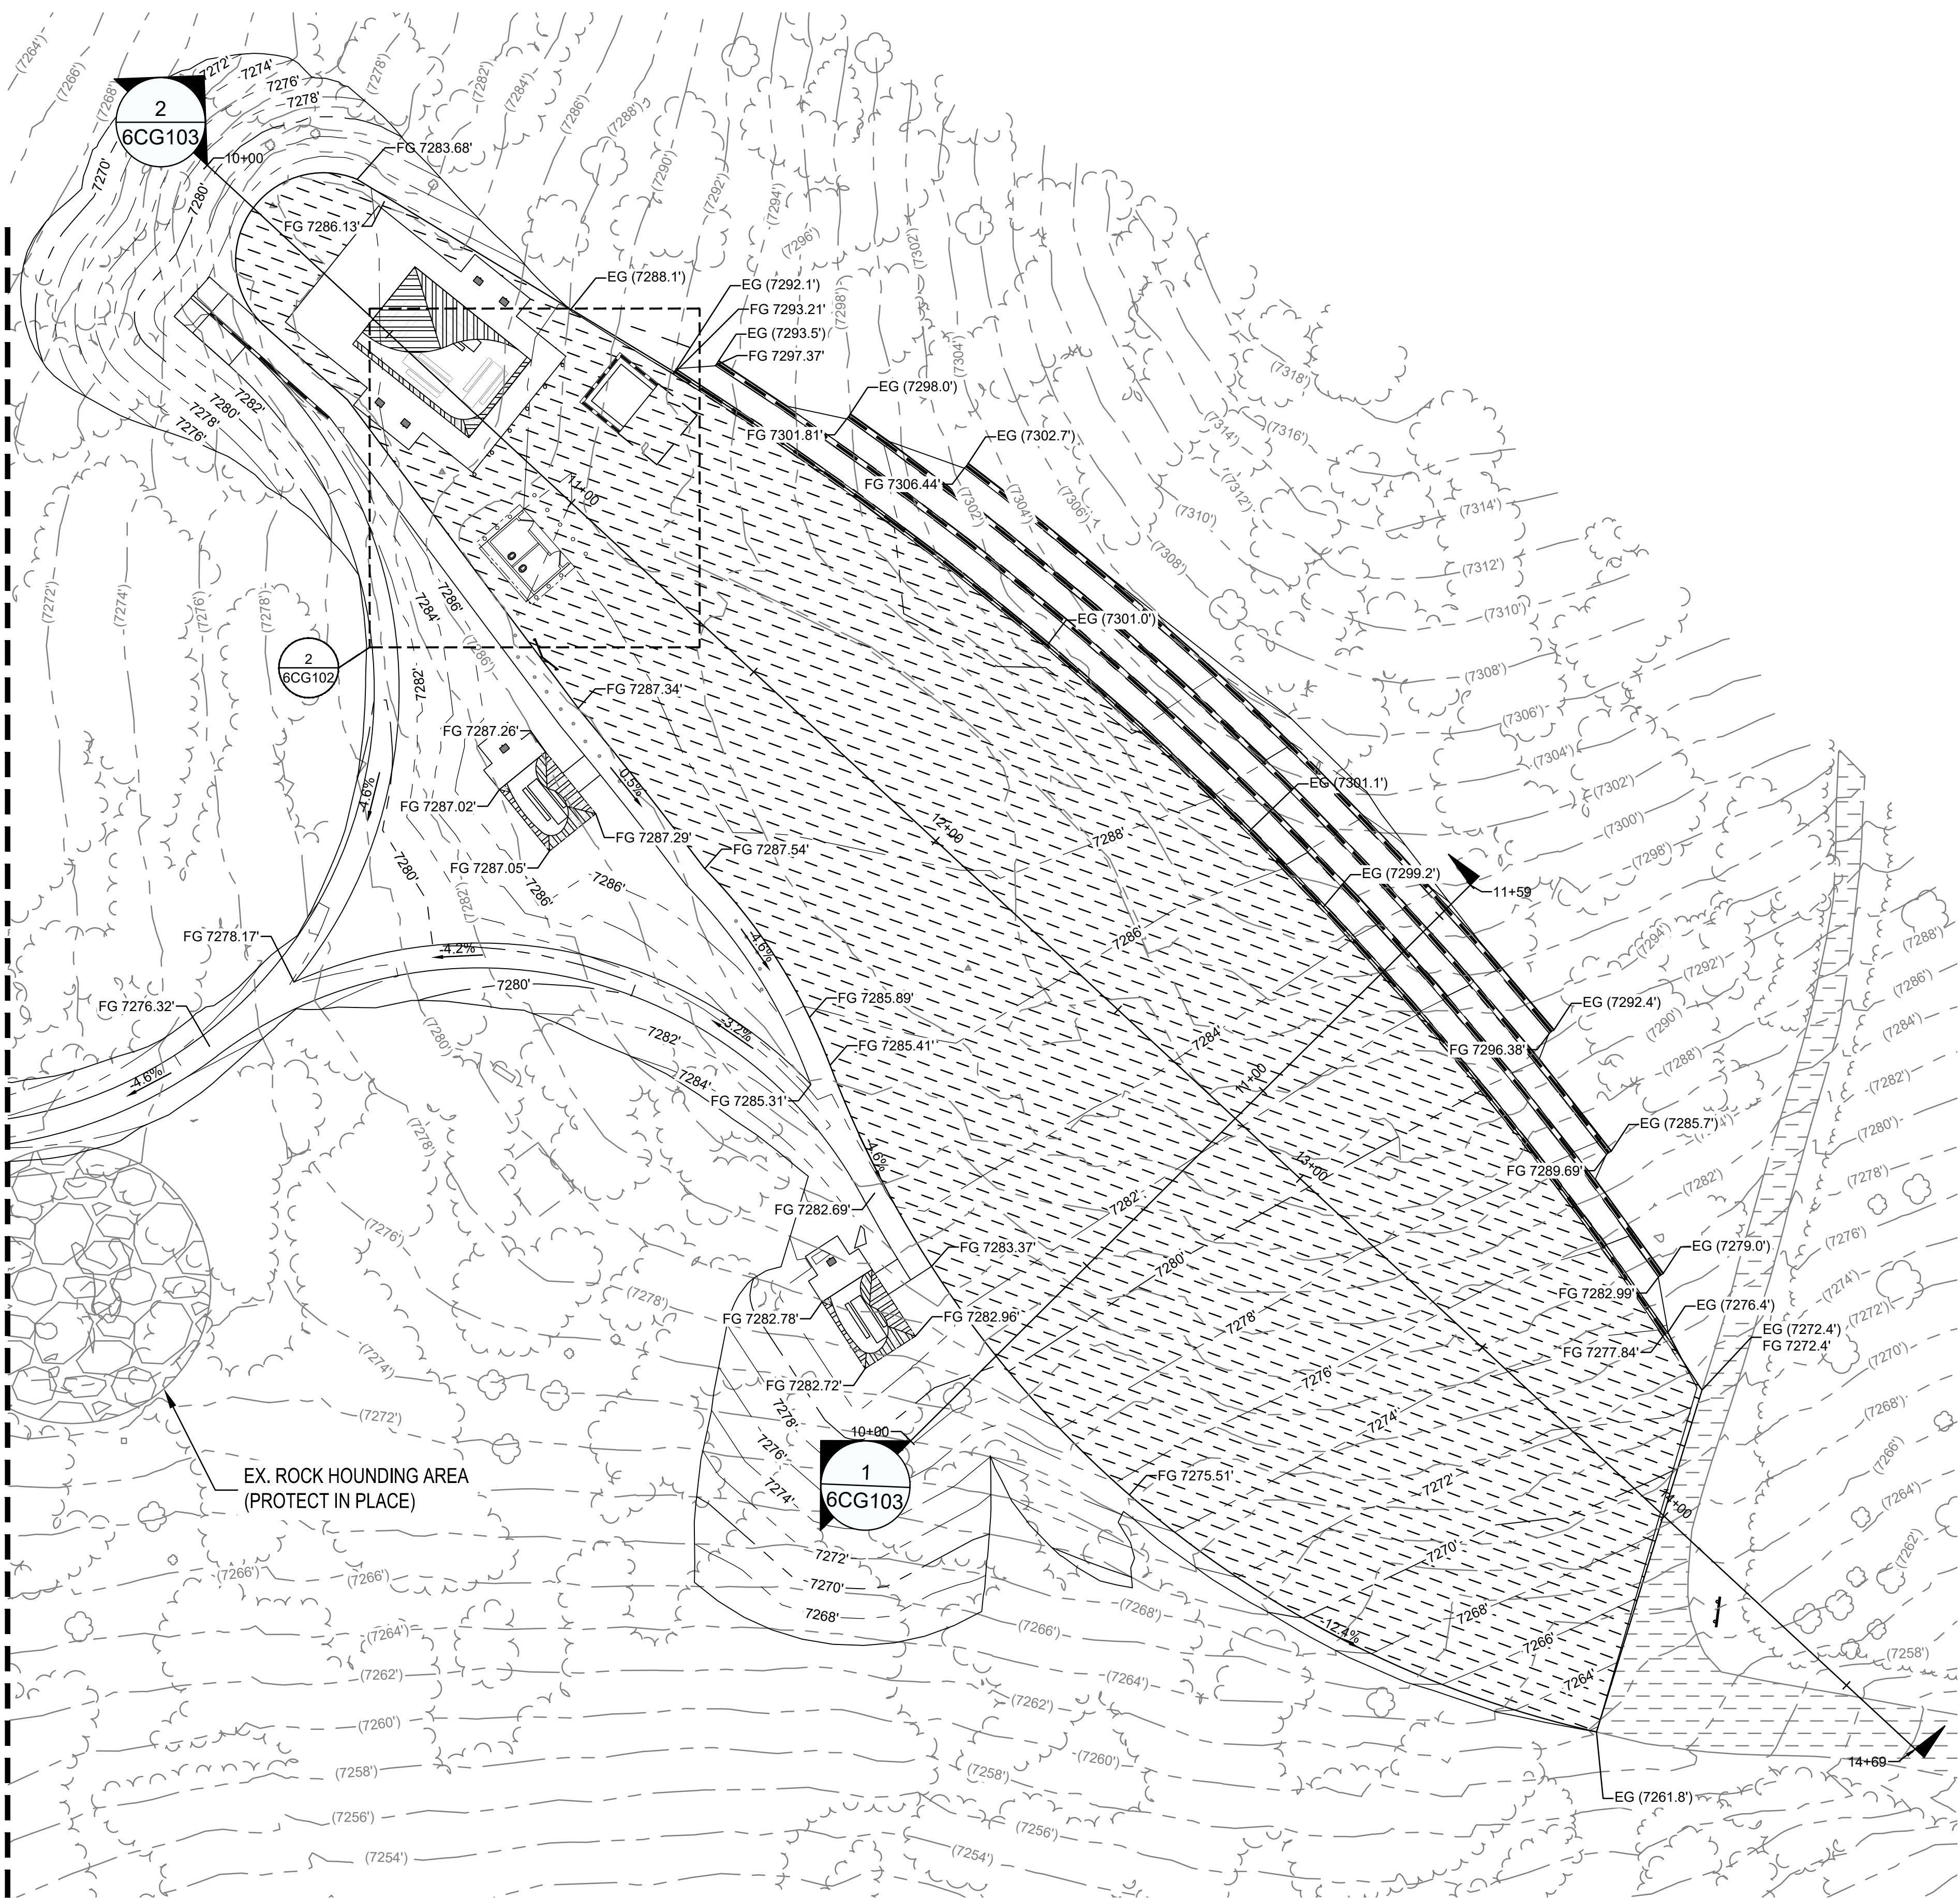


GARNET HILL MAIN TRAIL PARKING AREA

1" = 20'

1
6CG102

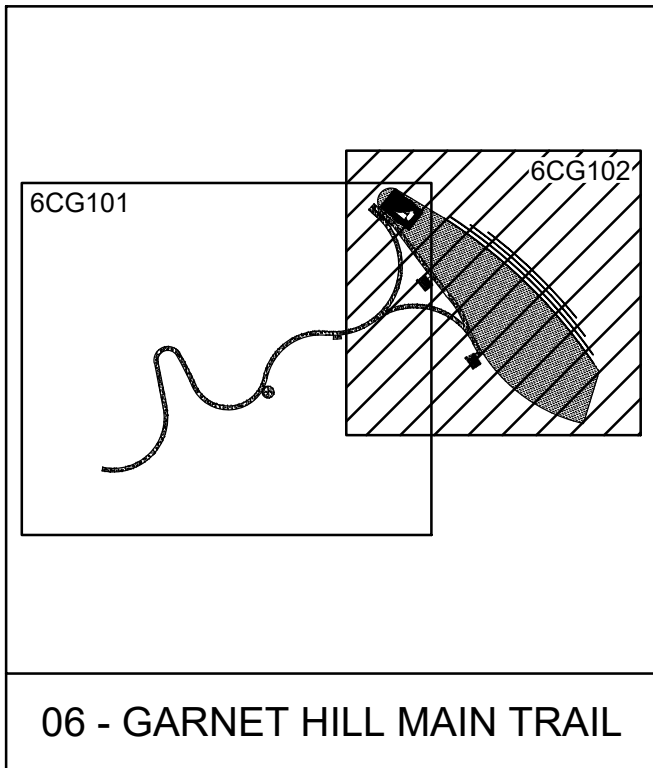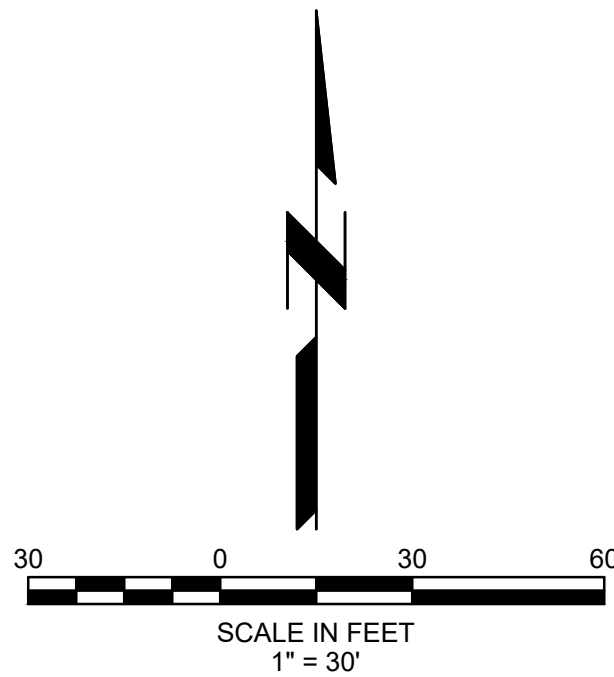


CUT/FILL VOLUMES	
CUT:	4970 CY
FILL:	1795 CY
NET:	3175 CY (CUT)

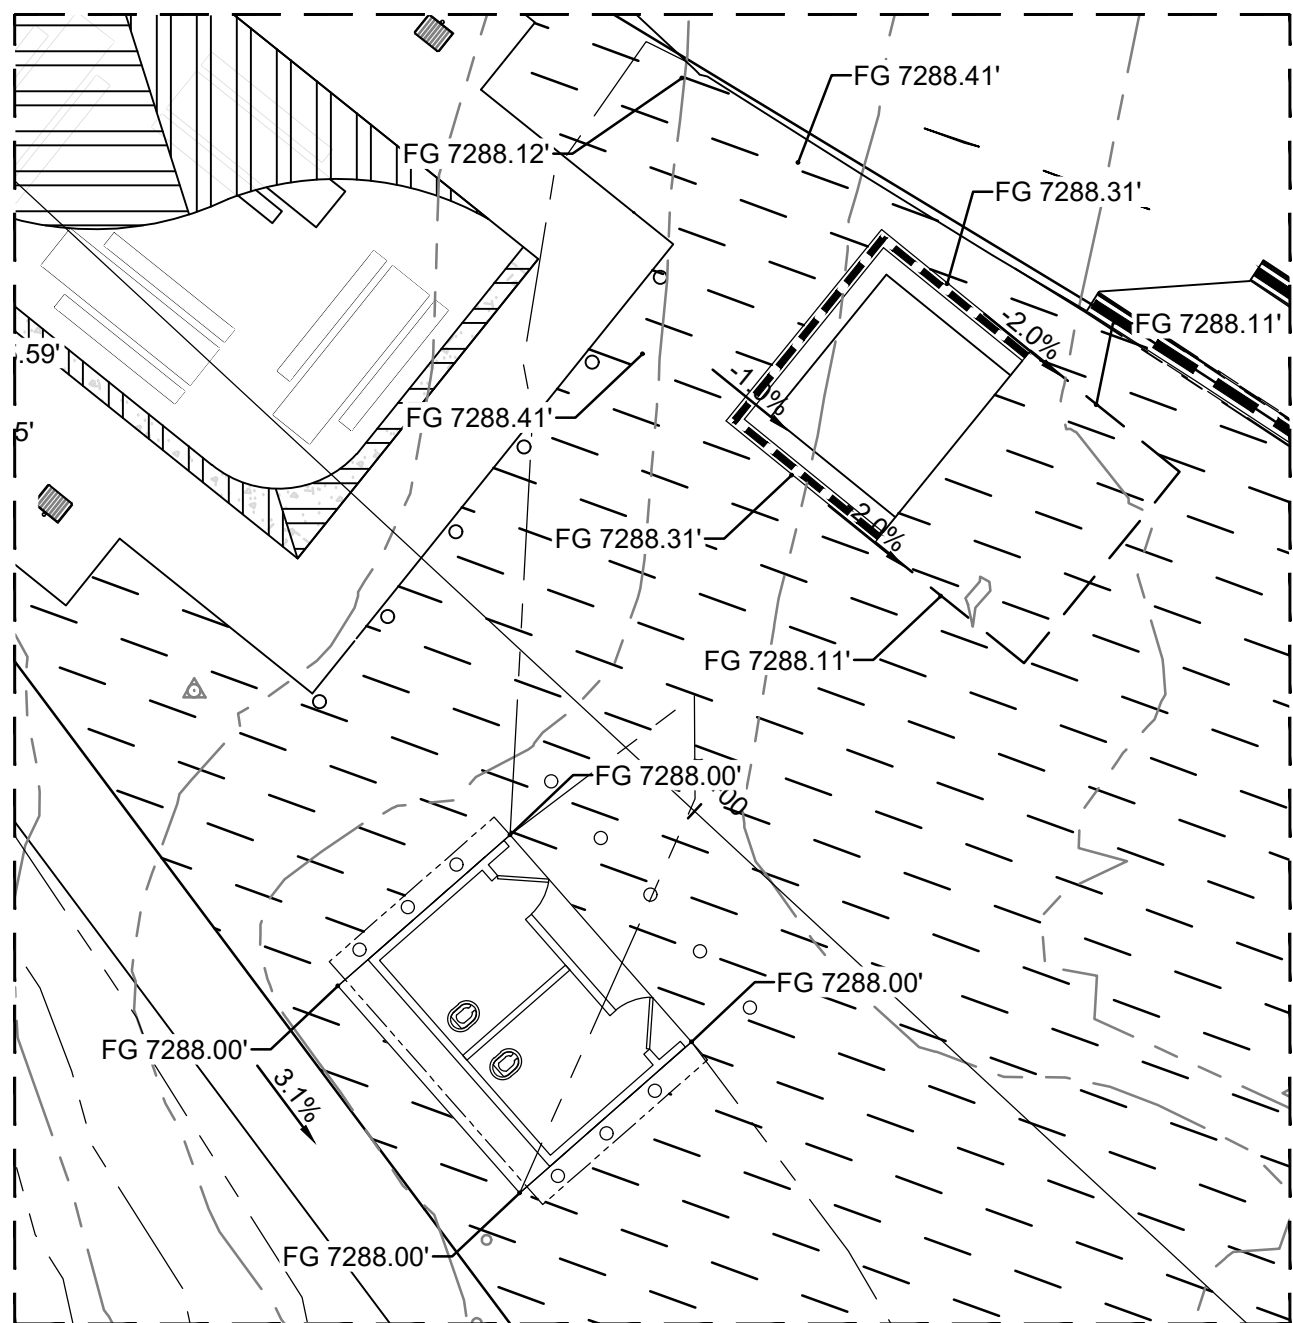

ENLARGED GRADING PLAN

1" = 10'

2
6CG102

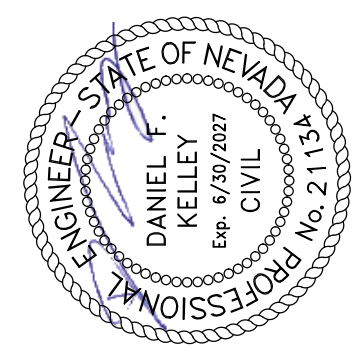

UNITED STATES DEPARTMENT OF THE INTERIOR
BUREAU OF LAND MANAGEMENT

GARNET HILL RECREATION AREA TITLE I AND II SERVICES

BUREAU OF LAND MANAGEMENT DISTRICT OFFICE
ELY, NEVADA

Project Status	Issue Date
100% CONSTRUCTION DOCUMENTS	12/16/2025
BLM Project #	140L0621D0006
Drawn By	A.BROWN
Checked By	D.KELLEY


Revision Issue	Date
Description	
Rev. #	

06 - GARNET HILL MAIN TRAIL
MAIN TRAIL GRADING PLAN 2

6CG102


19 Dec 2025

P:\Projects\BLM - NV & CA\IDOTask Orders\Task 27 - Garnet Hill Recreation Area Title 1 & II Services\Engineering\Drawings\Production Drawings\06 - GARNET HILL MAIN TRAIL HEAD\208-003-06-CG.dwg 12/16/2025 8:15 AM ABBROWN

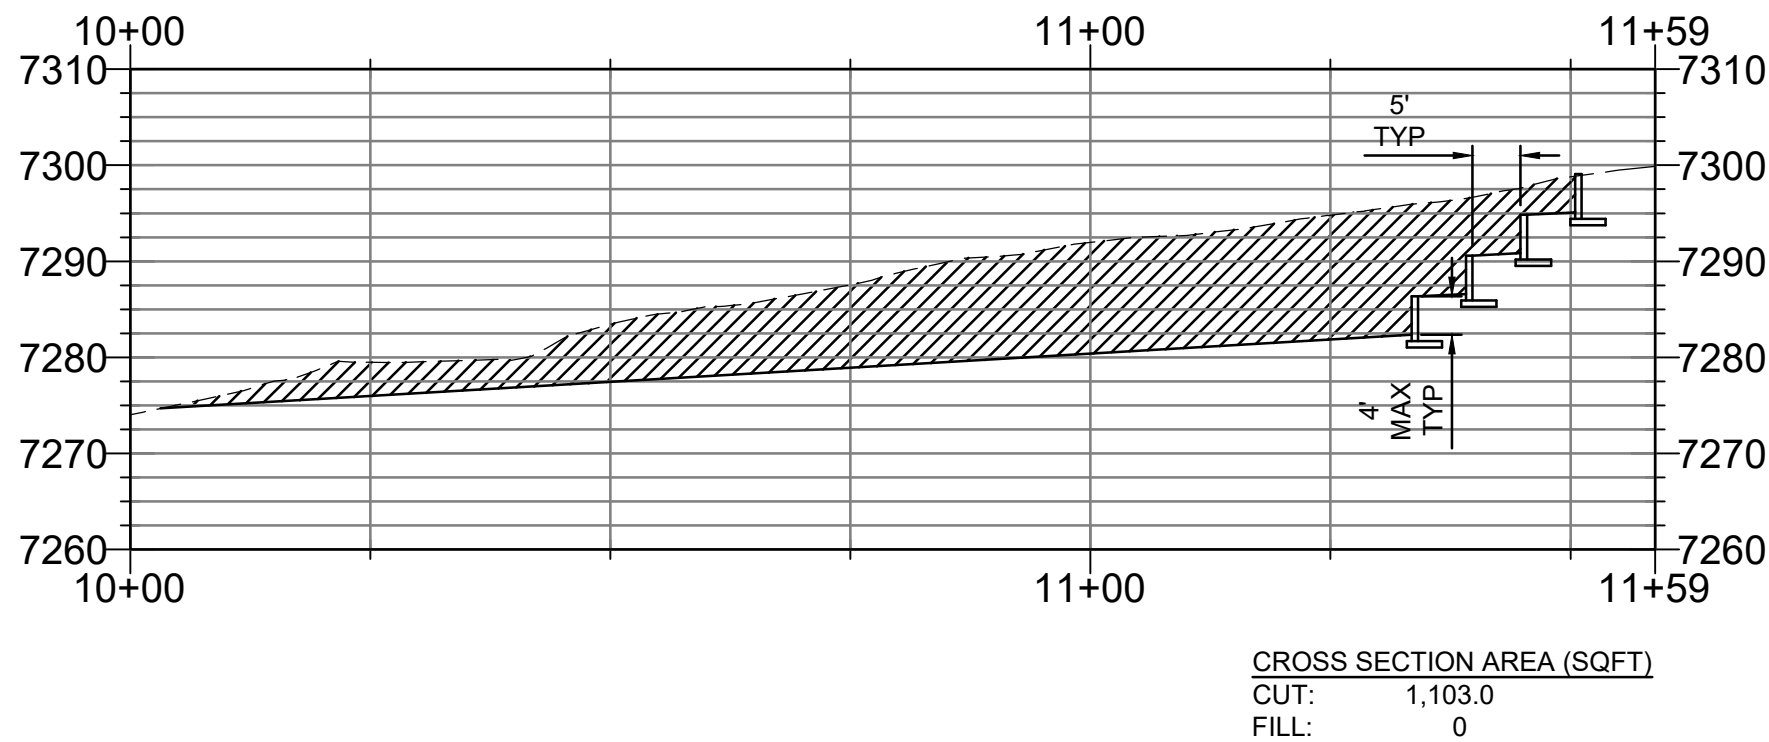



SECTION 1
HOR 1" = 20' | VERT 1" = 20'

1
6CG102

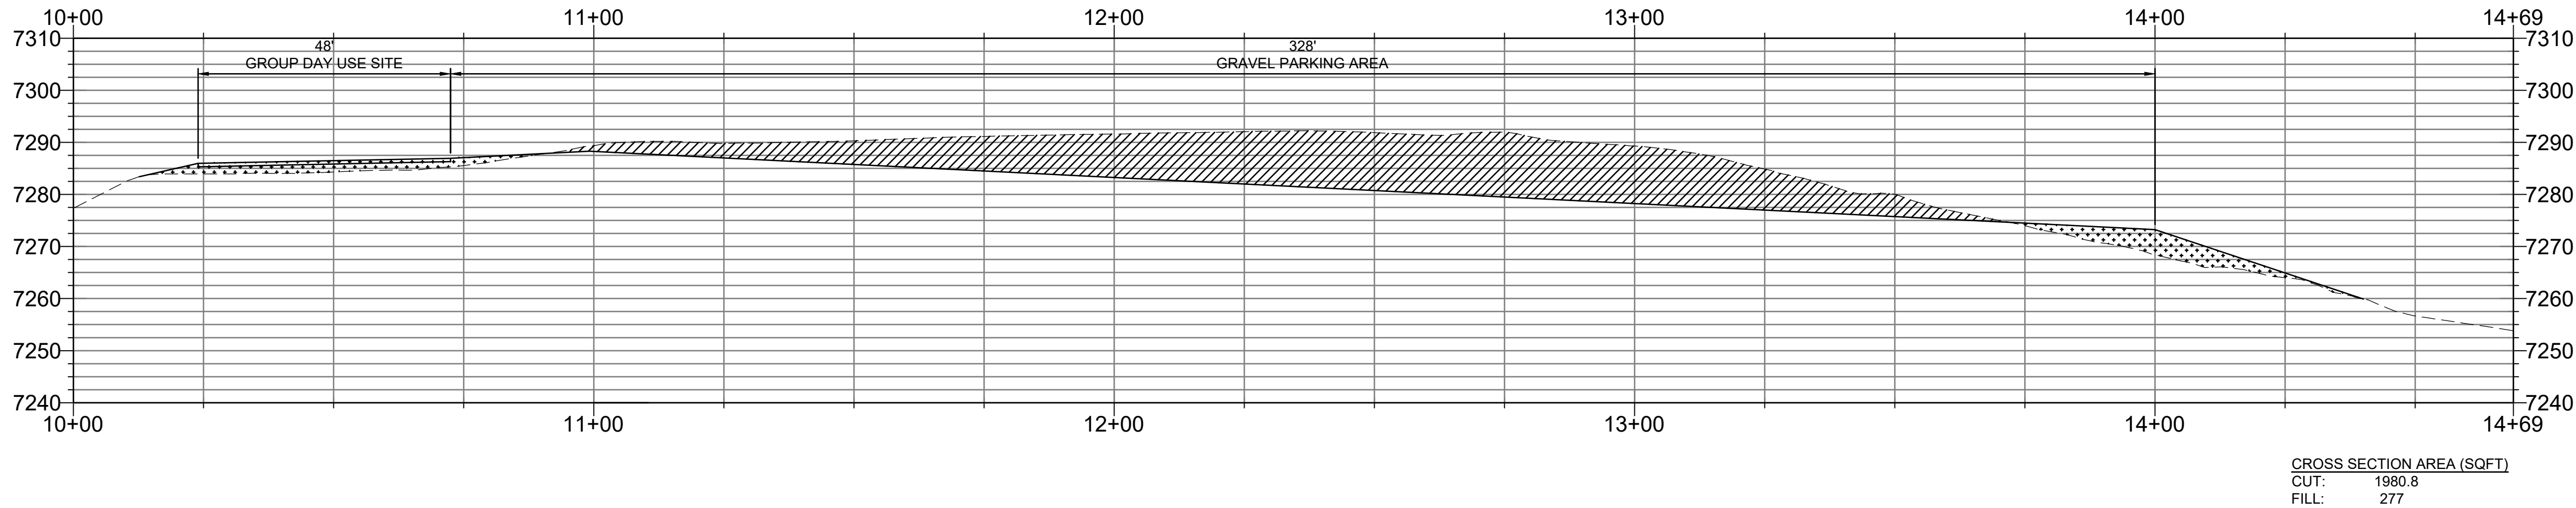

SECTION 2
HOR 1" = 20' | VERT 1" = 20'

2
6CG102

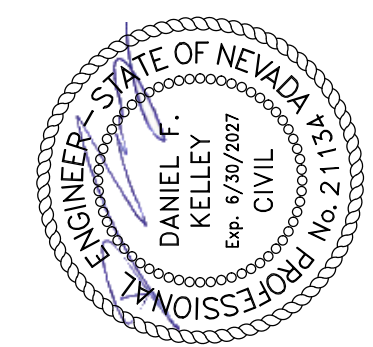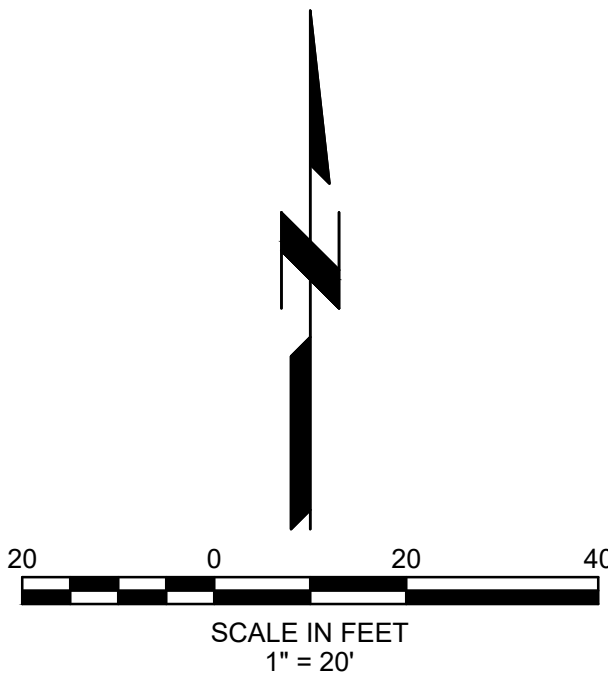

UNITED STATES DEPARTMENT OF THE INTERIOR
BUREAU OF LAND MANAGEMENT

GARNET HILL RECREATION AREA TITLE I AND II SERVICES



BUREAU OF LAND MANAGEMENT DISTRICT OFFICE
ELY, NEVADA

Rev. #	Revision Issue Description	Date	Project Status	Issue Date
			100% CONSTRUCTION DOCUMENTS	12/16/2025
			BLM Project #	140L0621D0006
			Drawn By	A.BROWN
			Checked By	D.KELLEY


06 - GARNET HILL MAIN TRAIL
MAIN TRAIL GRADING SECTIONS

6CG103

P:\Projects\BLM - NV & CA IDOT\Task Orders\Task 27 - Garnet Hill Recreation Area\Task 27 - Garnet Hill Recreation Area Title I & II Services\Engineering\Drawings\Production Drawings\07 - ROAD\208-203-07-CP.dwg, 12/16/2025 8:16 AM ABBROWN

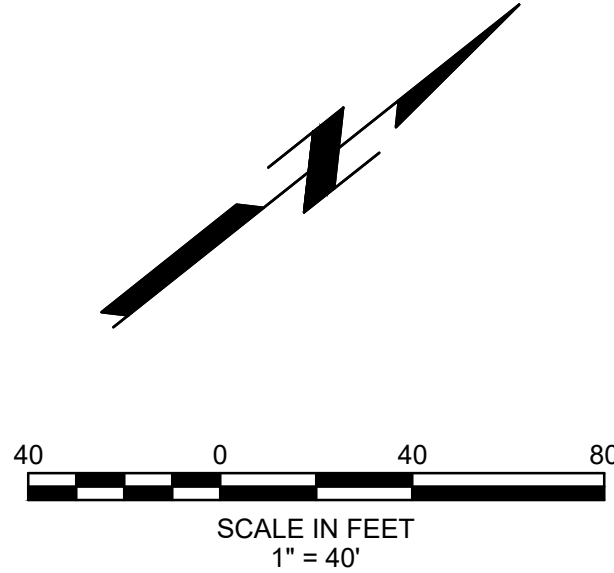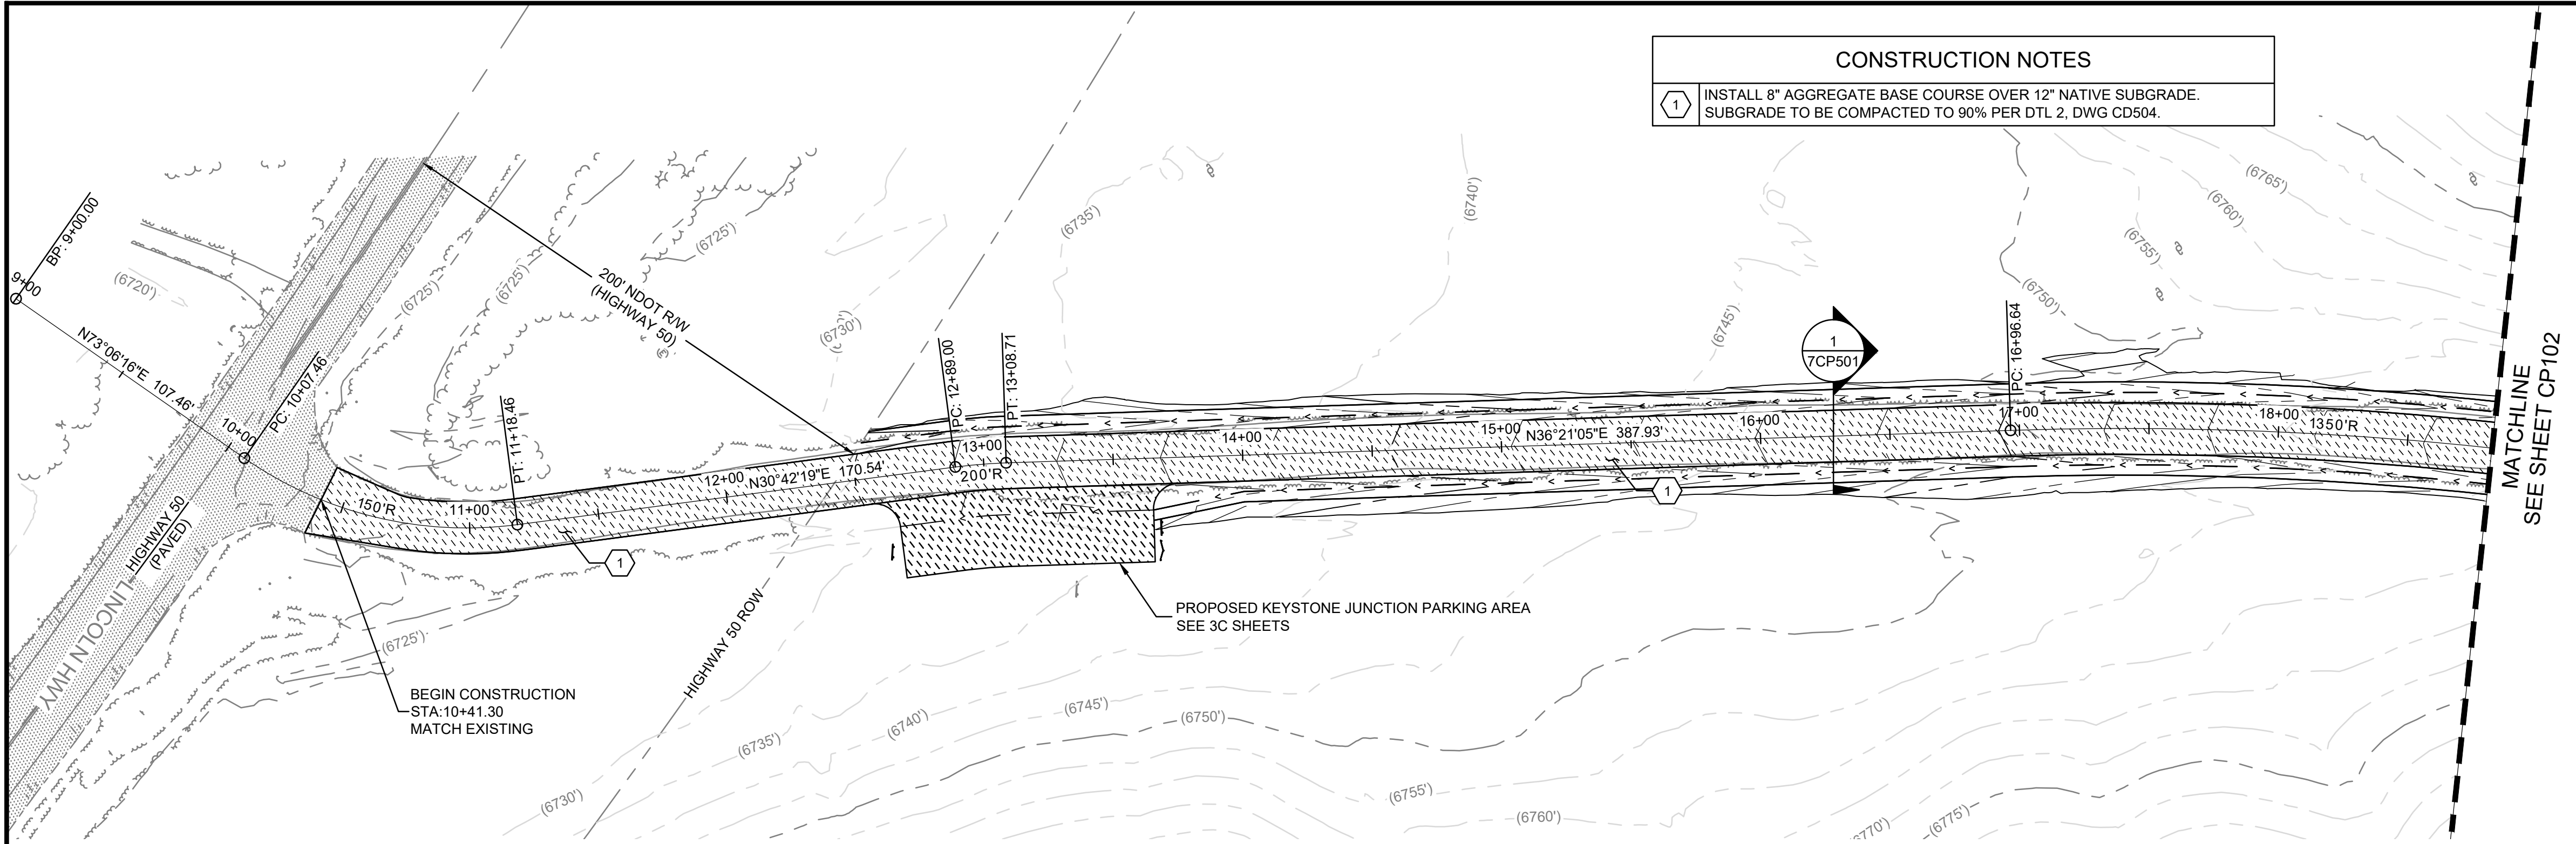


CUT/FILL VOLUMES	
CUT:	1,855 CY
FILL:	4,255 CY
NET:	2,400 CY (FILL)

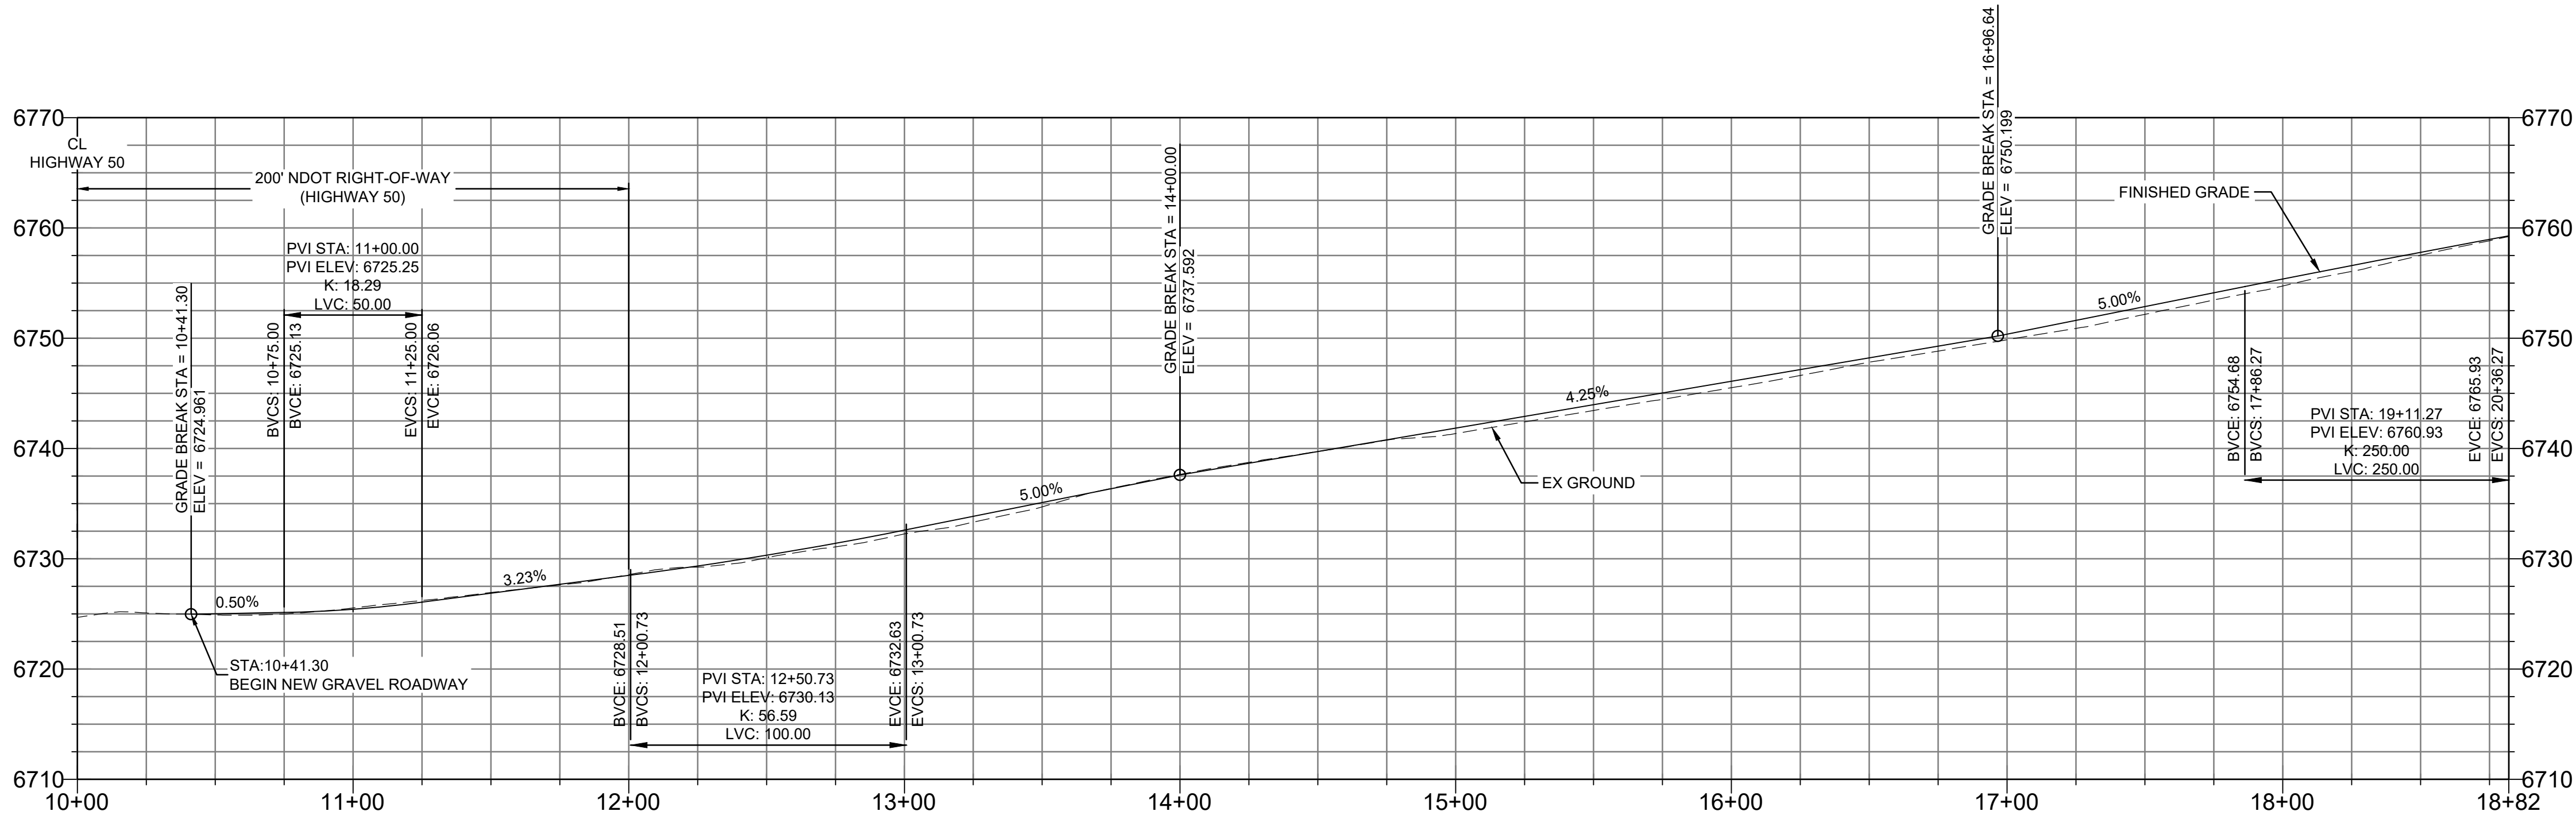

POLE LINE ROAD PLAN & PROFILE

HORIZ: 1" = 40' | VERT: 1" = 4'

1
7CP101

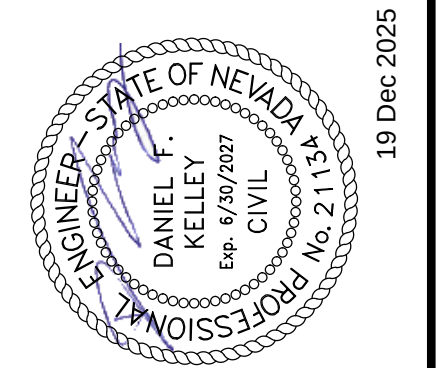

UNITED STATES DEPARTMENT OF THE INTERIOR
BUREAU OF LAND MANAGEMENT

**GARNET HILL RECREATION AREA TITLE I
AND II SERVICES**

BUREAU OF LAND MANAGEMENT DISTRICT OFFICE
ELY, NEVADA





Project Status	Issue Date
100% CONSTRUCTION DOCUMENTS	12/16/2025
BLM Project #	Drawn By
140L0621 D0006	ABBROWN
Checked By	D.KELLEY

Revision Issue	Date
Description	
Rev. #	

07 - POLE LINE ROAD
POLE LINE ROAD PLAN &
PROFILE

7CP101

P:\Projects\BLM - NV & CA ID\Task Orders\Task 27 - Garnet Hill Recreation Area Title I & II Services\Engineering\Drawings\Production Drawings\07 - ROAD\208-203-07-CP.dwg 12/16/2025 8:16 AM A.BROWN

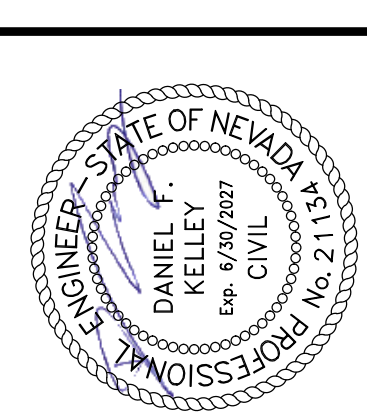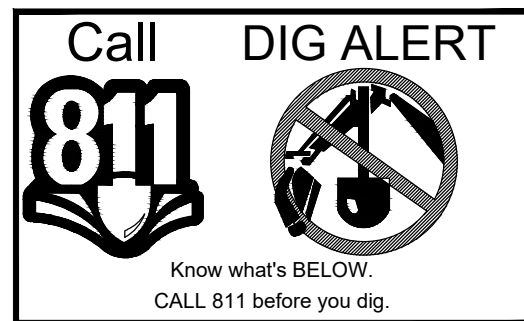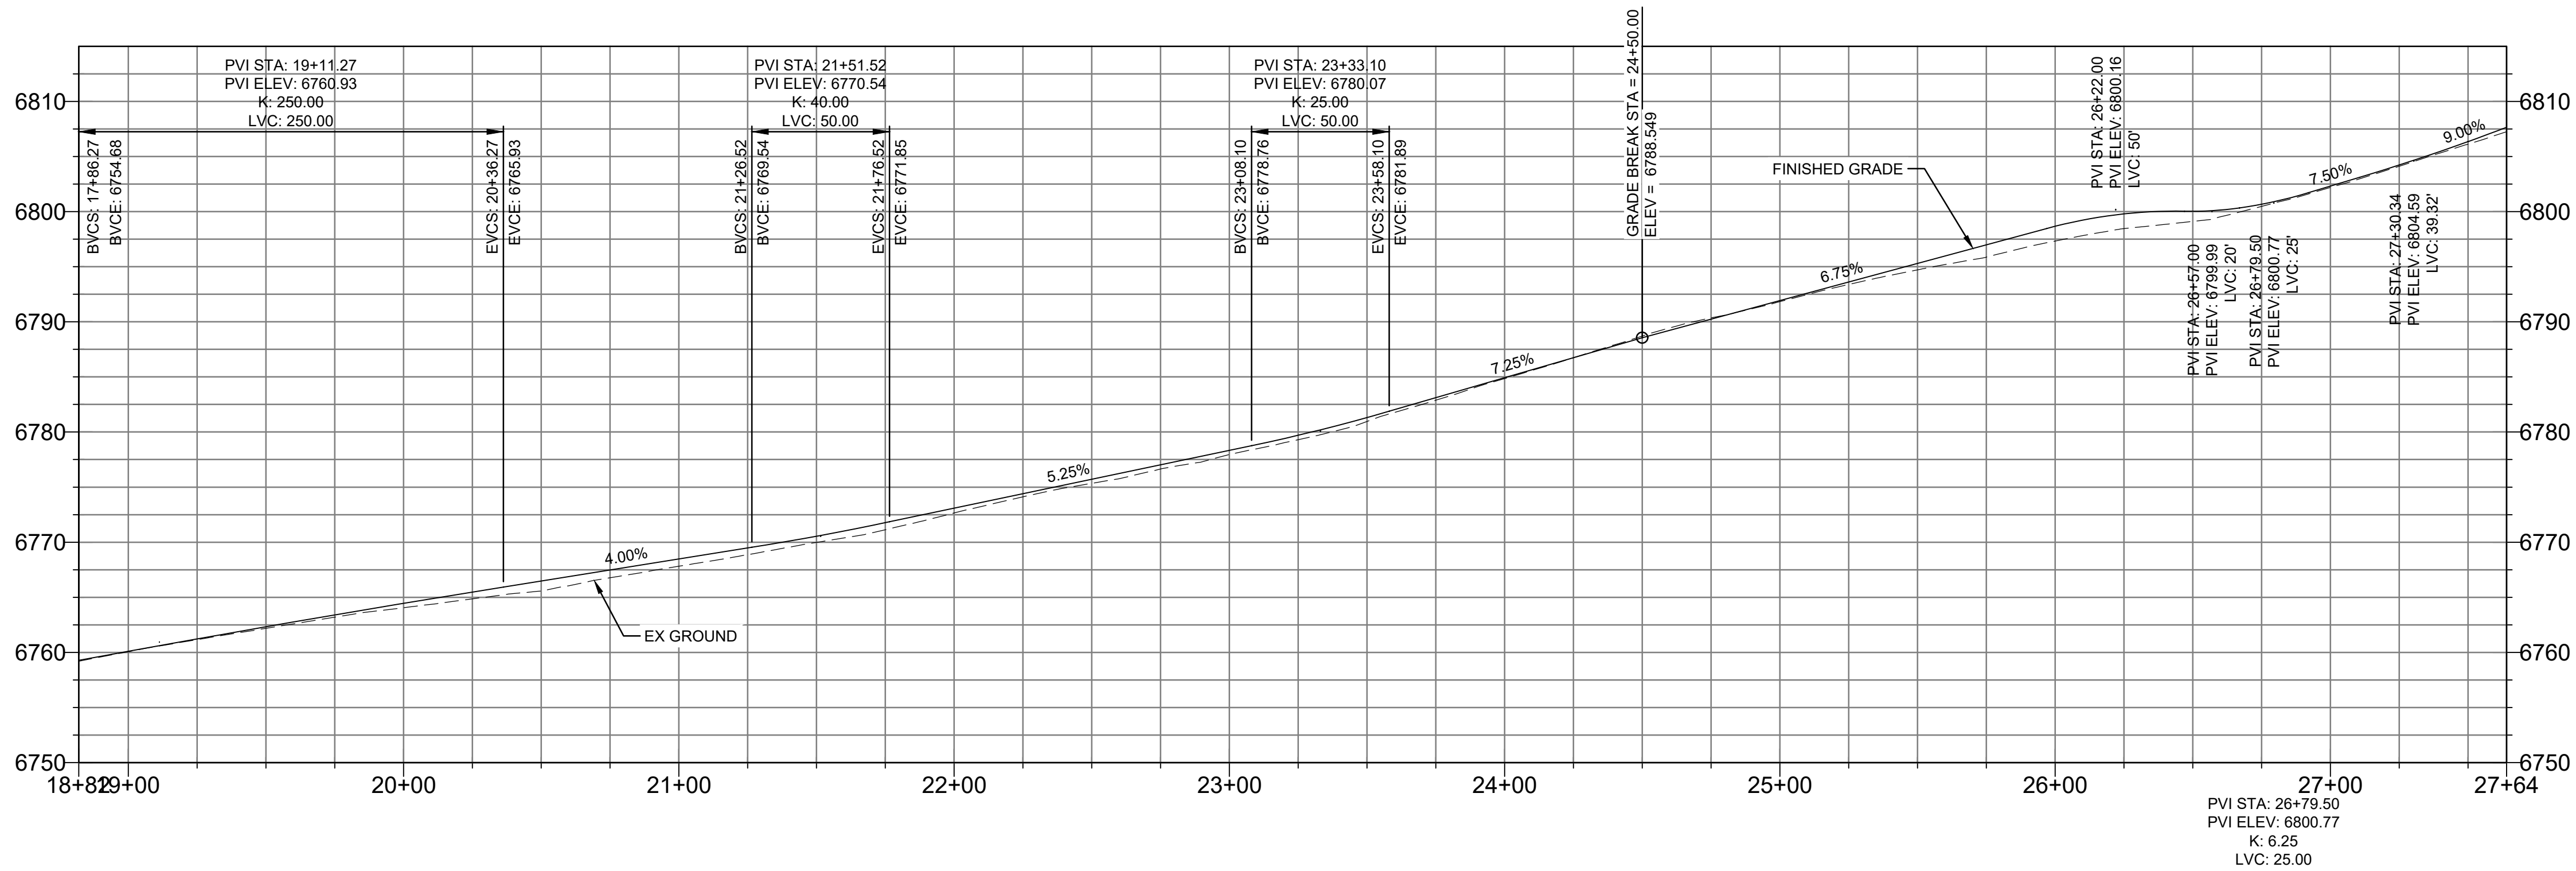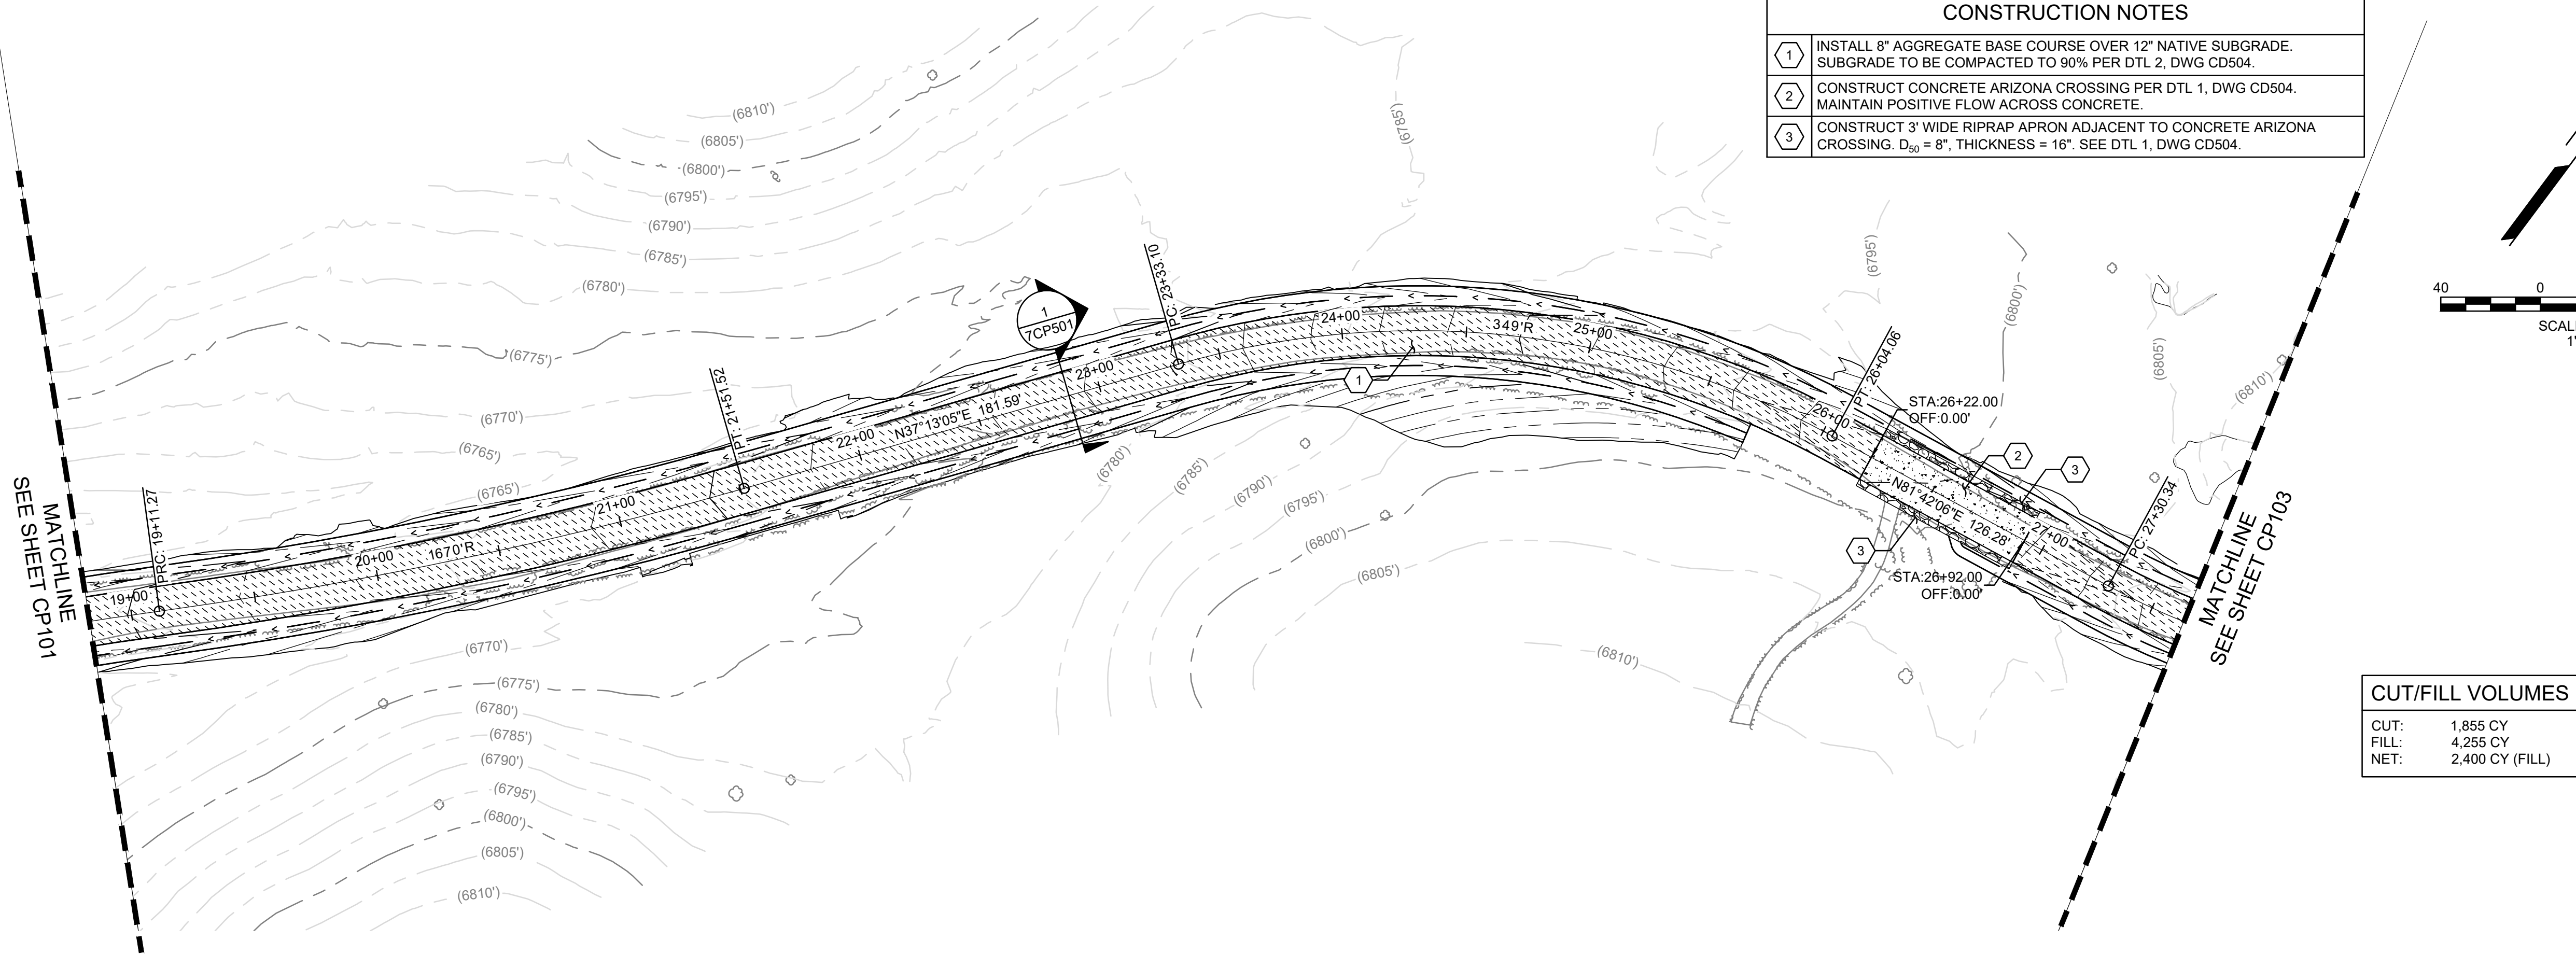

UNITED STATES DEPARTMENT OF THE INTERIOR
BUREAU OF LAND MANAGEMENT

**GARNET HILL RECREATION AREA TITLE I
AND II SERVICES**


BUREAU OF LAND MANAGEMENT DISTRICT OFFICE
ELY, NEVADA

Project Status
100% CONSTRUCTION DOCUMENTS
BLM Project # 140L0621D0006
Drawn By A.BROWN
Checked By D.KELLEY


Revision Issue
Date Description
Rev. #

07 - POLE LINE ROAD
POLE LINE ROAD PLAN &
PROFILE
7CP102

P:\Projects\BLM - NV & CA ID\Task Orders\Task 27 - Garnet Hill Recreation Area\Task 27 - Garnet Hill Recreation Area Title I & II Services\Engineering\Drawings\Production Drawings\07 - ROAD\208-203-07-CP.dwg 12/16/2025 8:16 AM ABBROWN

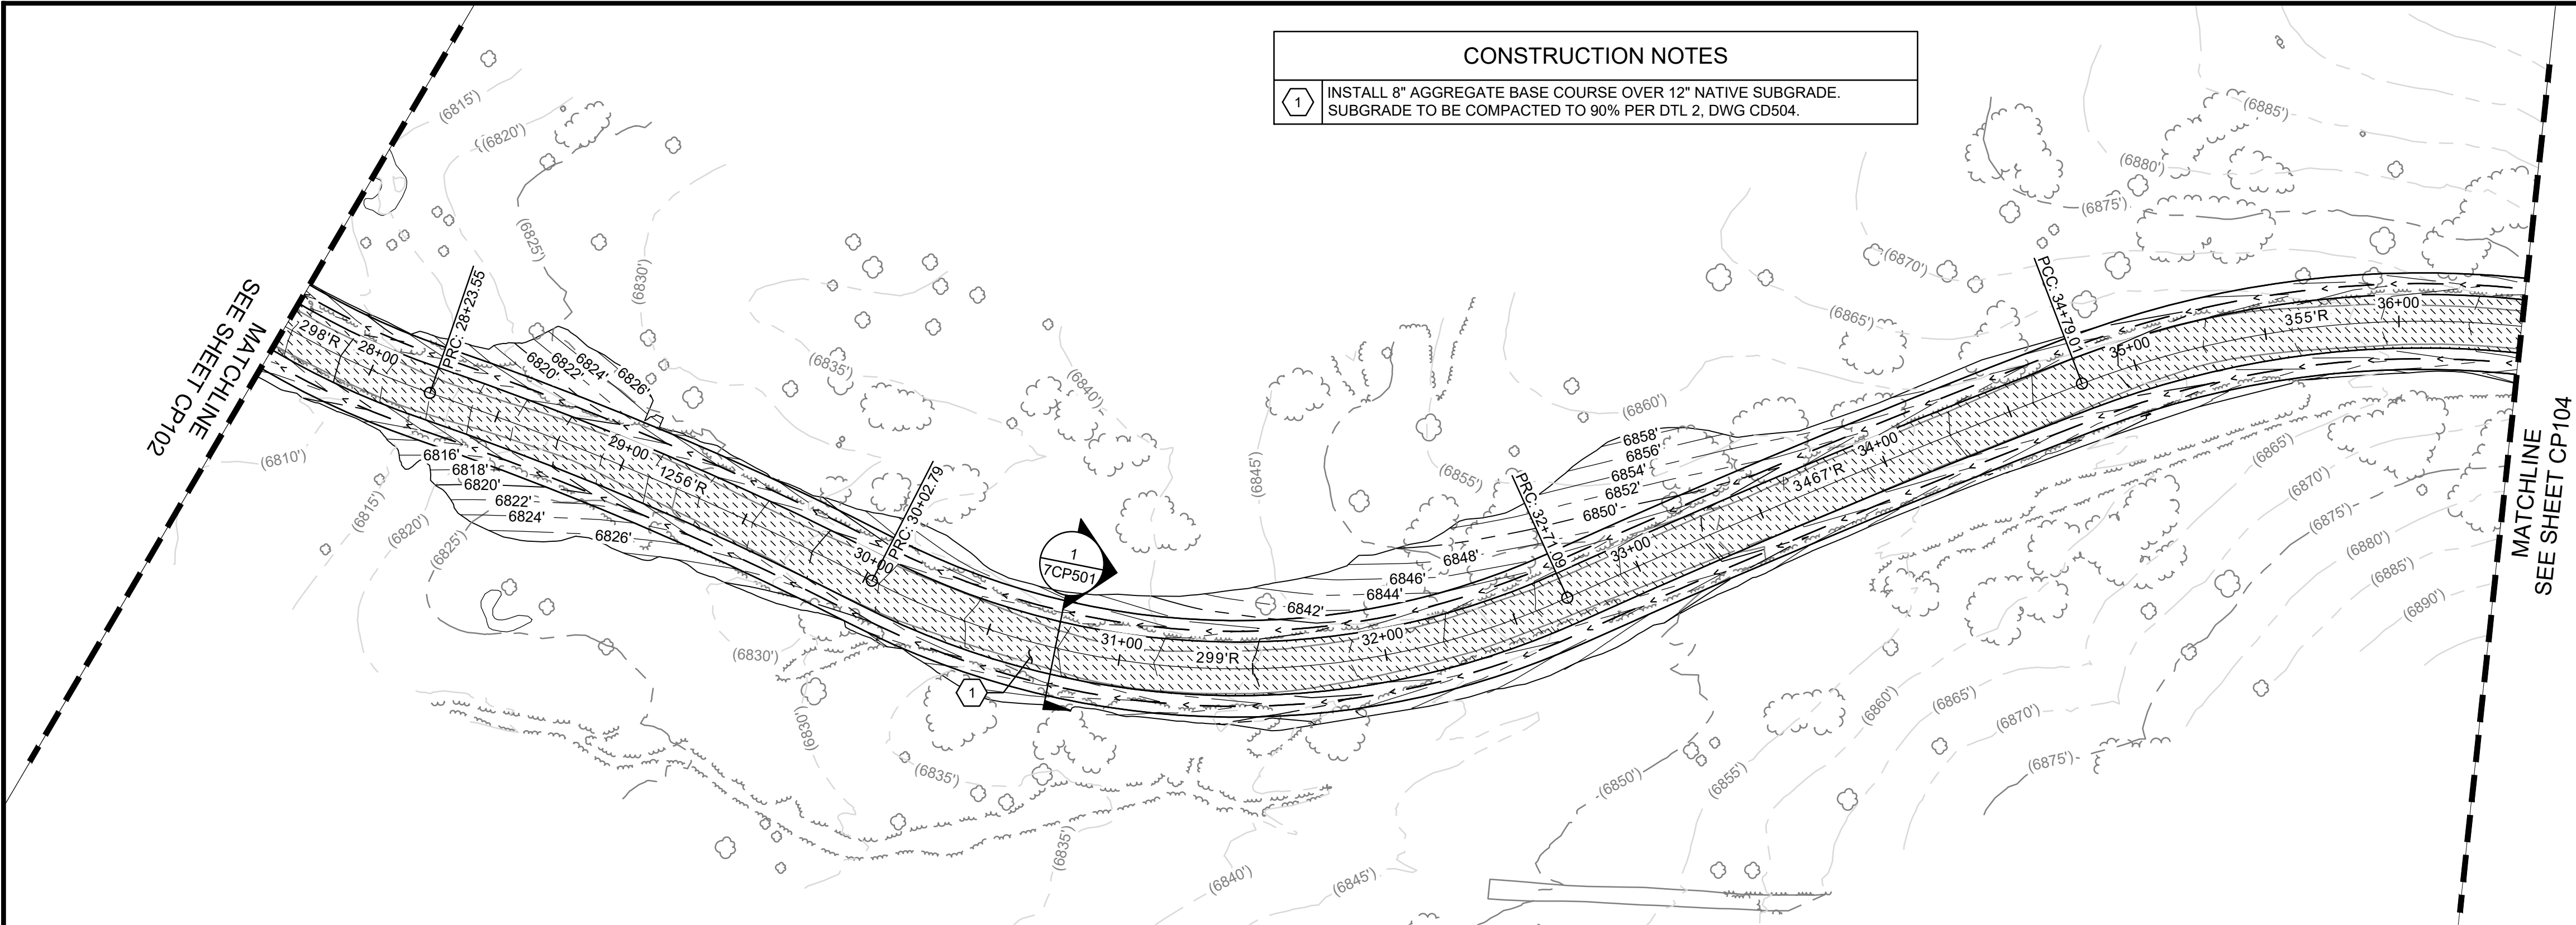


CUT/FILL VOLUMES	
CUT:	1,855 CY
FILL:	4,255 CY
NET:	2,400 CY (FILL)

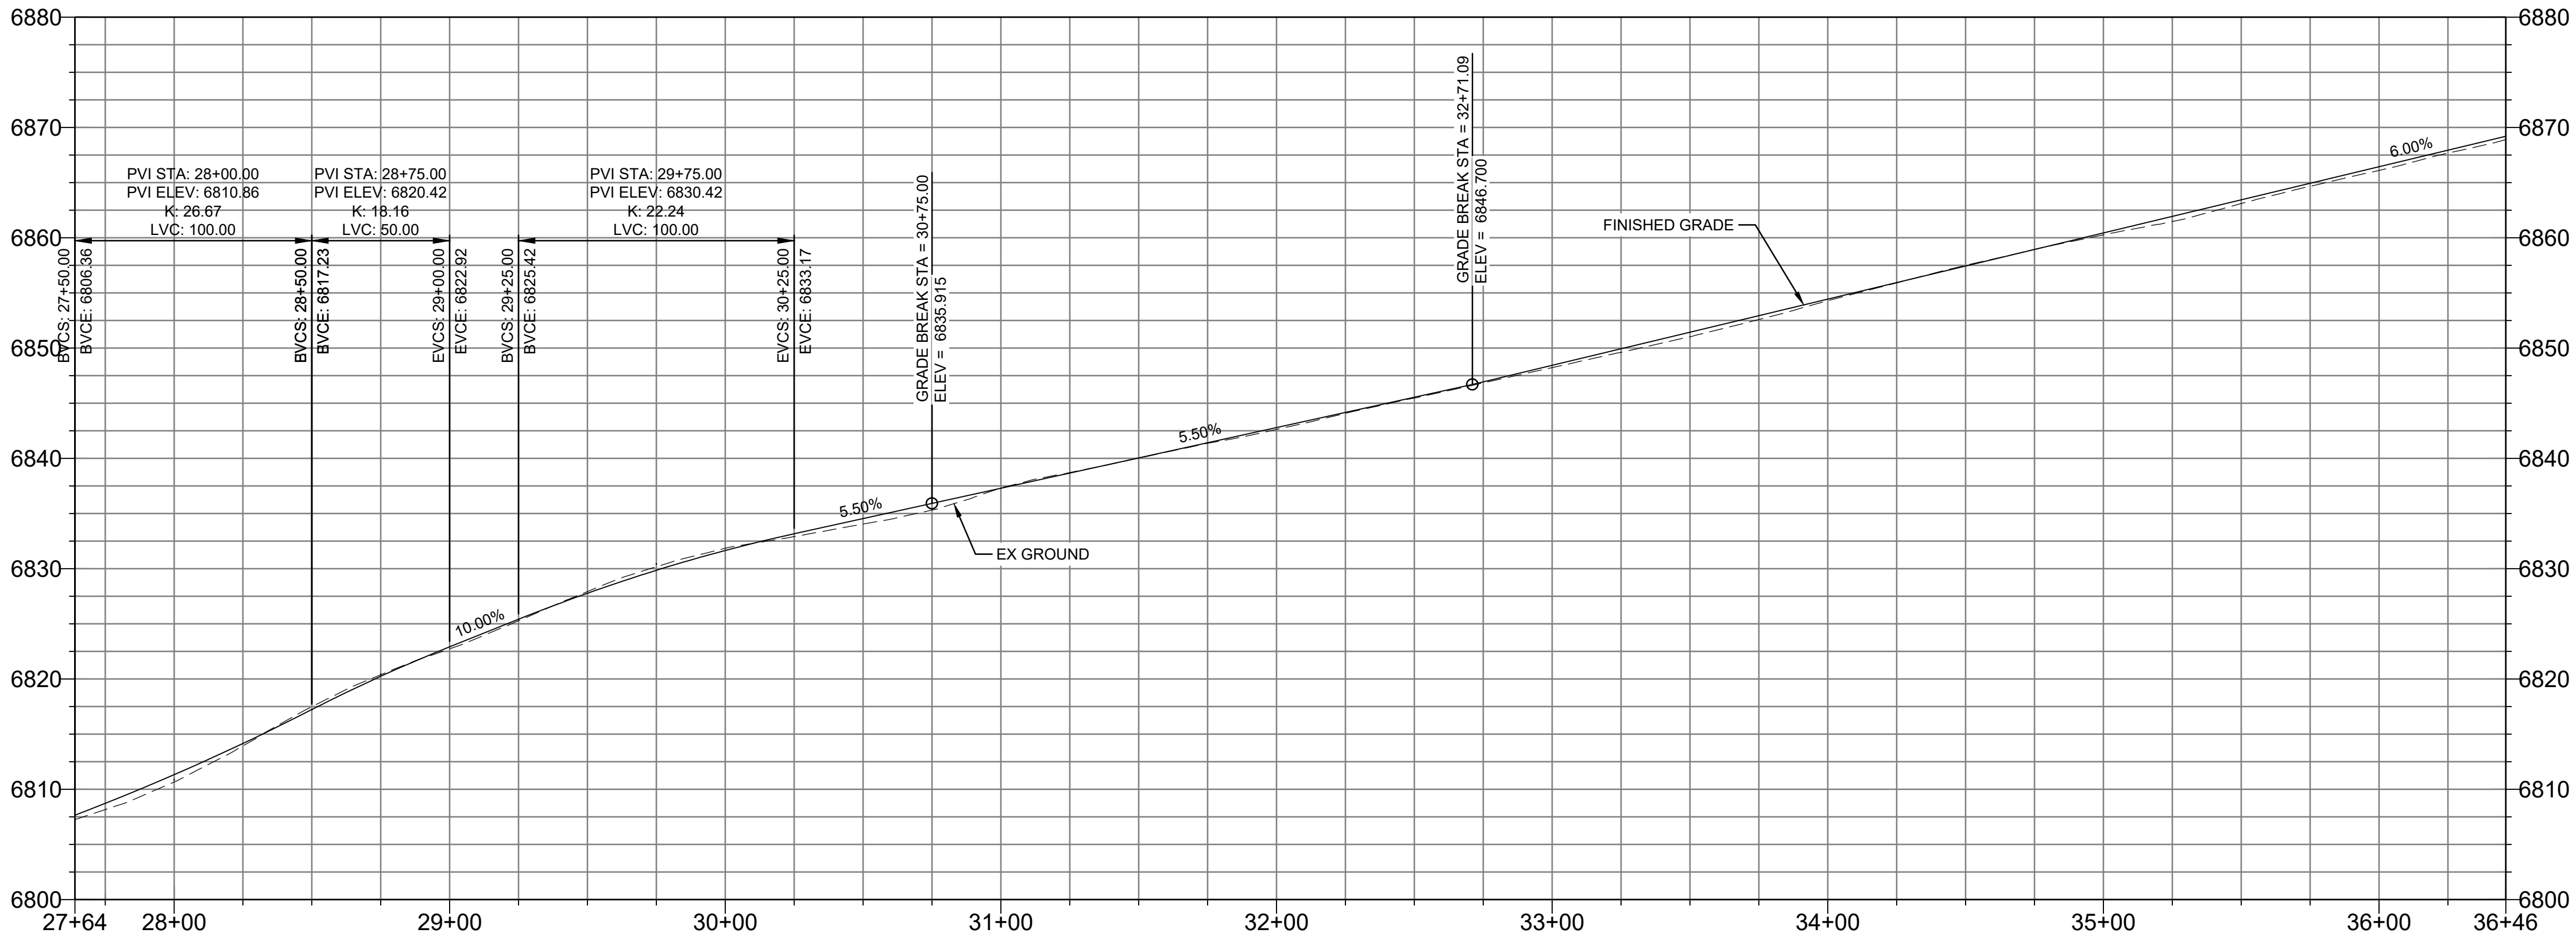

POLE LINE ROAD PLAN & PROFILE
HORIZ: 1" = 40' | VERT: 1" = 4'

1
7CP103



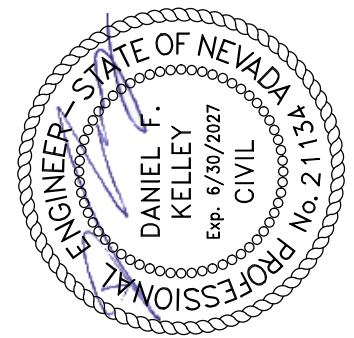

UNITED STATES DEPARTMENT OF THE INTERIOR
BUREAU OF LAND MANAGEMENT

**GARNET HILL RECREATION AREA TITLE I
AND II SERVICES**

BUREAU OF LAND MANAGEMENT DISTRICT OFFICE
ELY, NEVADA



Project Status	Issue Date
100% CONSTRUCTION DOCUMENTS	12/16/2025
BLM Project #	140L0621D0006
Drawn By	ABBROWN
Checked By	D.KELLEY

07 - POLE LINE ROAD
POLE LINE ROAD PLAN &
PROFILE

7CP103

19 Dec 2025

P:\Projects\BLM - NV & CA\IDOT\Task Orders\Task 27 - Garnet Hill Recreation Area\Task 1 & I Services\Engineering\Drawings\Production Drawings\07 - ROAD\208-203-07-CP.dwg 12/16/2025 8:16 AM A.BROWN

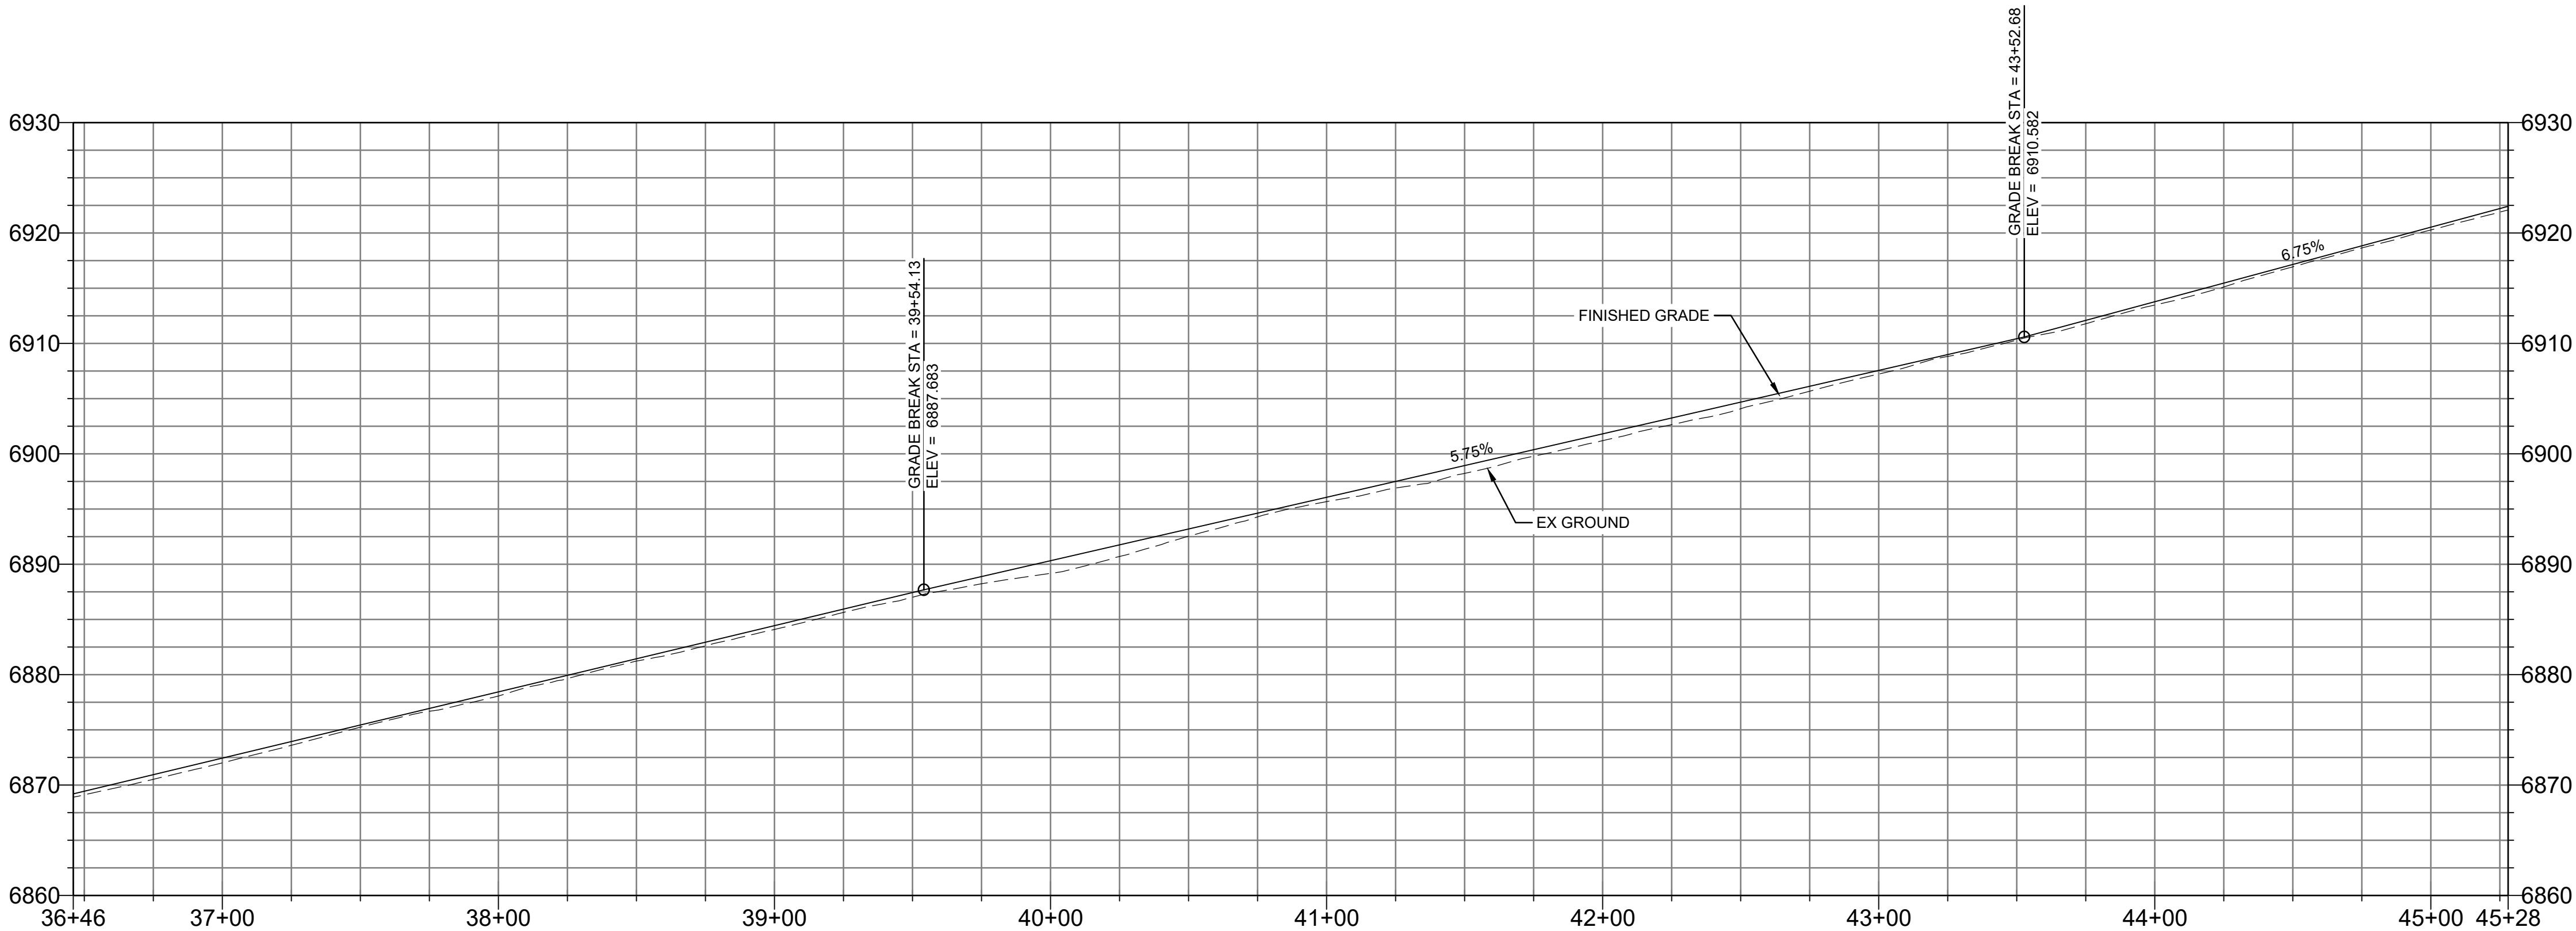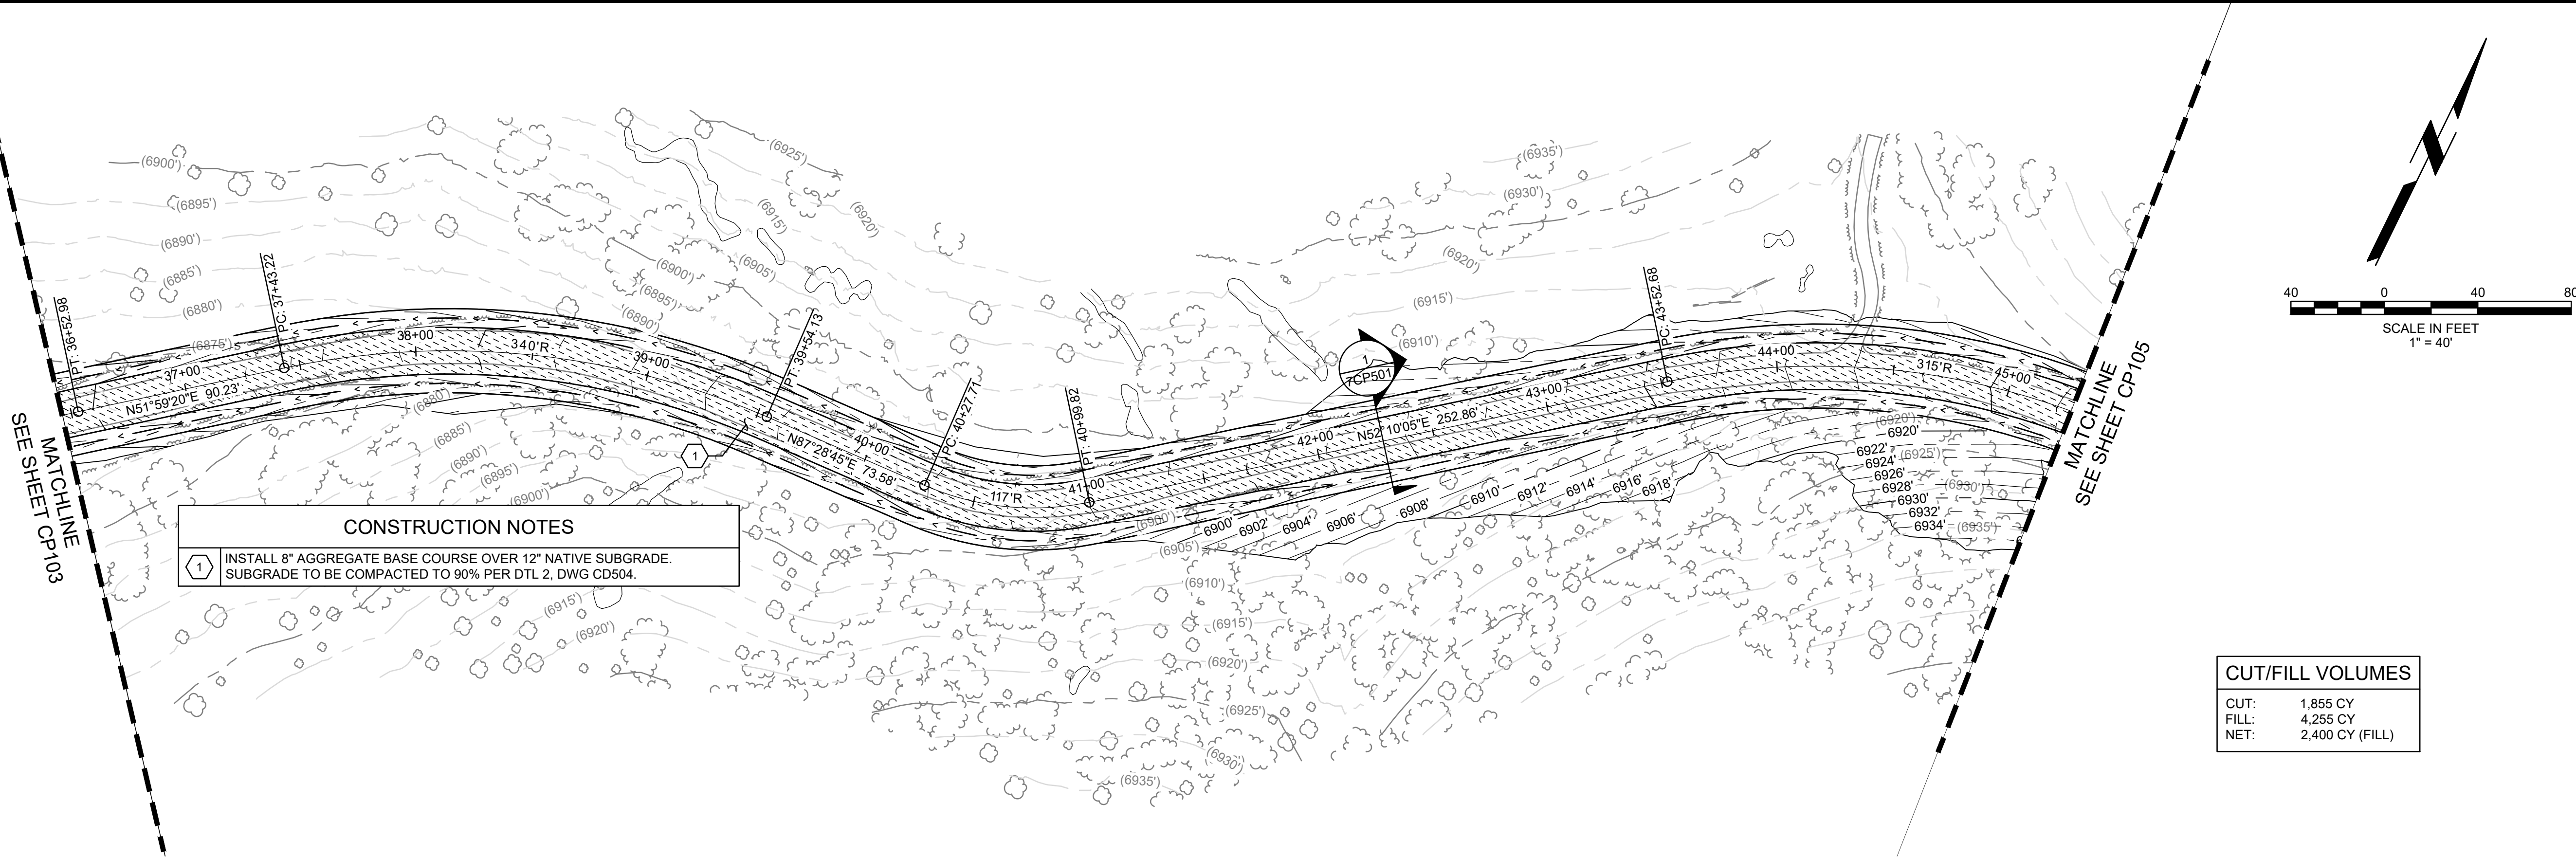

POLE LINE ROAD PLAN & PROFILE
HORIZ: 1" = 40' | VERT: 1" = 4'

1
7CP104



UNITED STATES DEPARTMENT OF THE INTERIOR
BUREAU OF LAND MANAGEMENT

GARNET HILL RECREATION AREA TITLE I AND II SERVICES

BUREAU OF LAND MANAGEMENT DISTRICT OFFICE
ELY, NEVADA



Project Status	Issue Date
	12/16/2025
100% CONSTRUCTION DOCUMENTS	BLM Project #
Drawn By	140L0621D0006
Checked By	A.BROWN
Rev. #	D.KELLEY

07 - POLE LINE ROAD
POLE LINE ROAD PLAN &
PROFILE

7CP104

19 Dec 2025

P:\Projects\BLM - NV & CA\IDOT\Task Orders\Task 27 - Garnet Hill Recreation Area\Task 27 - I Services\Engineering\Drawings\Production Drawings\07 - ROAD\208-203-07-CP.dwg, 12/16/2025 8:16 AM ABBROWN

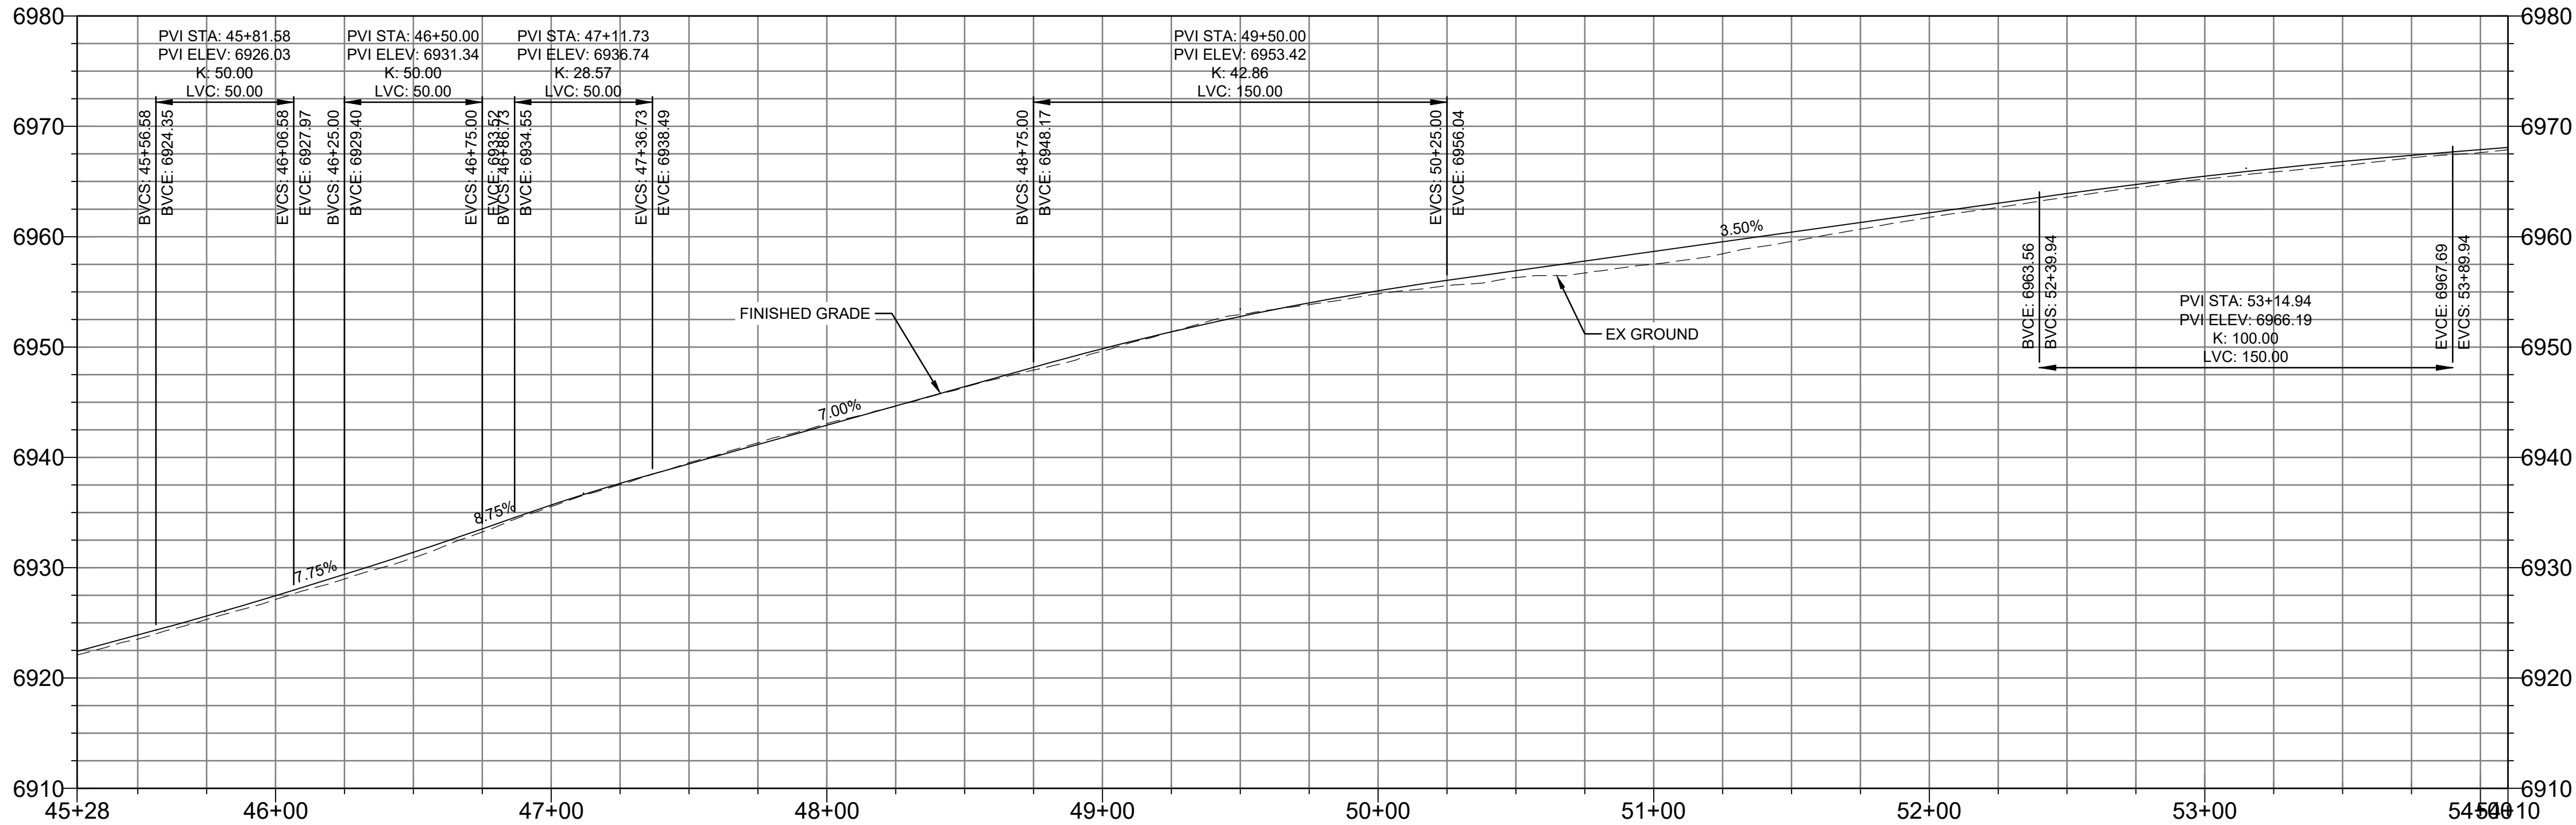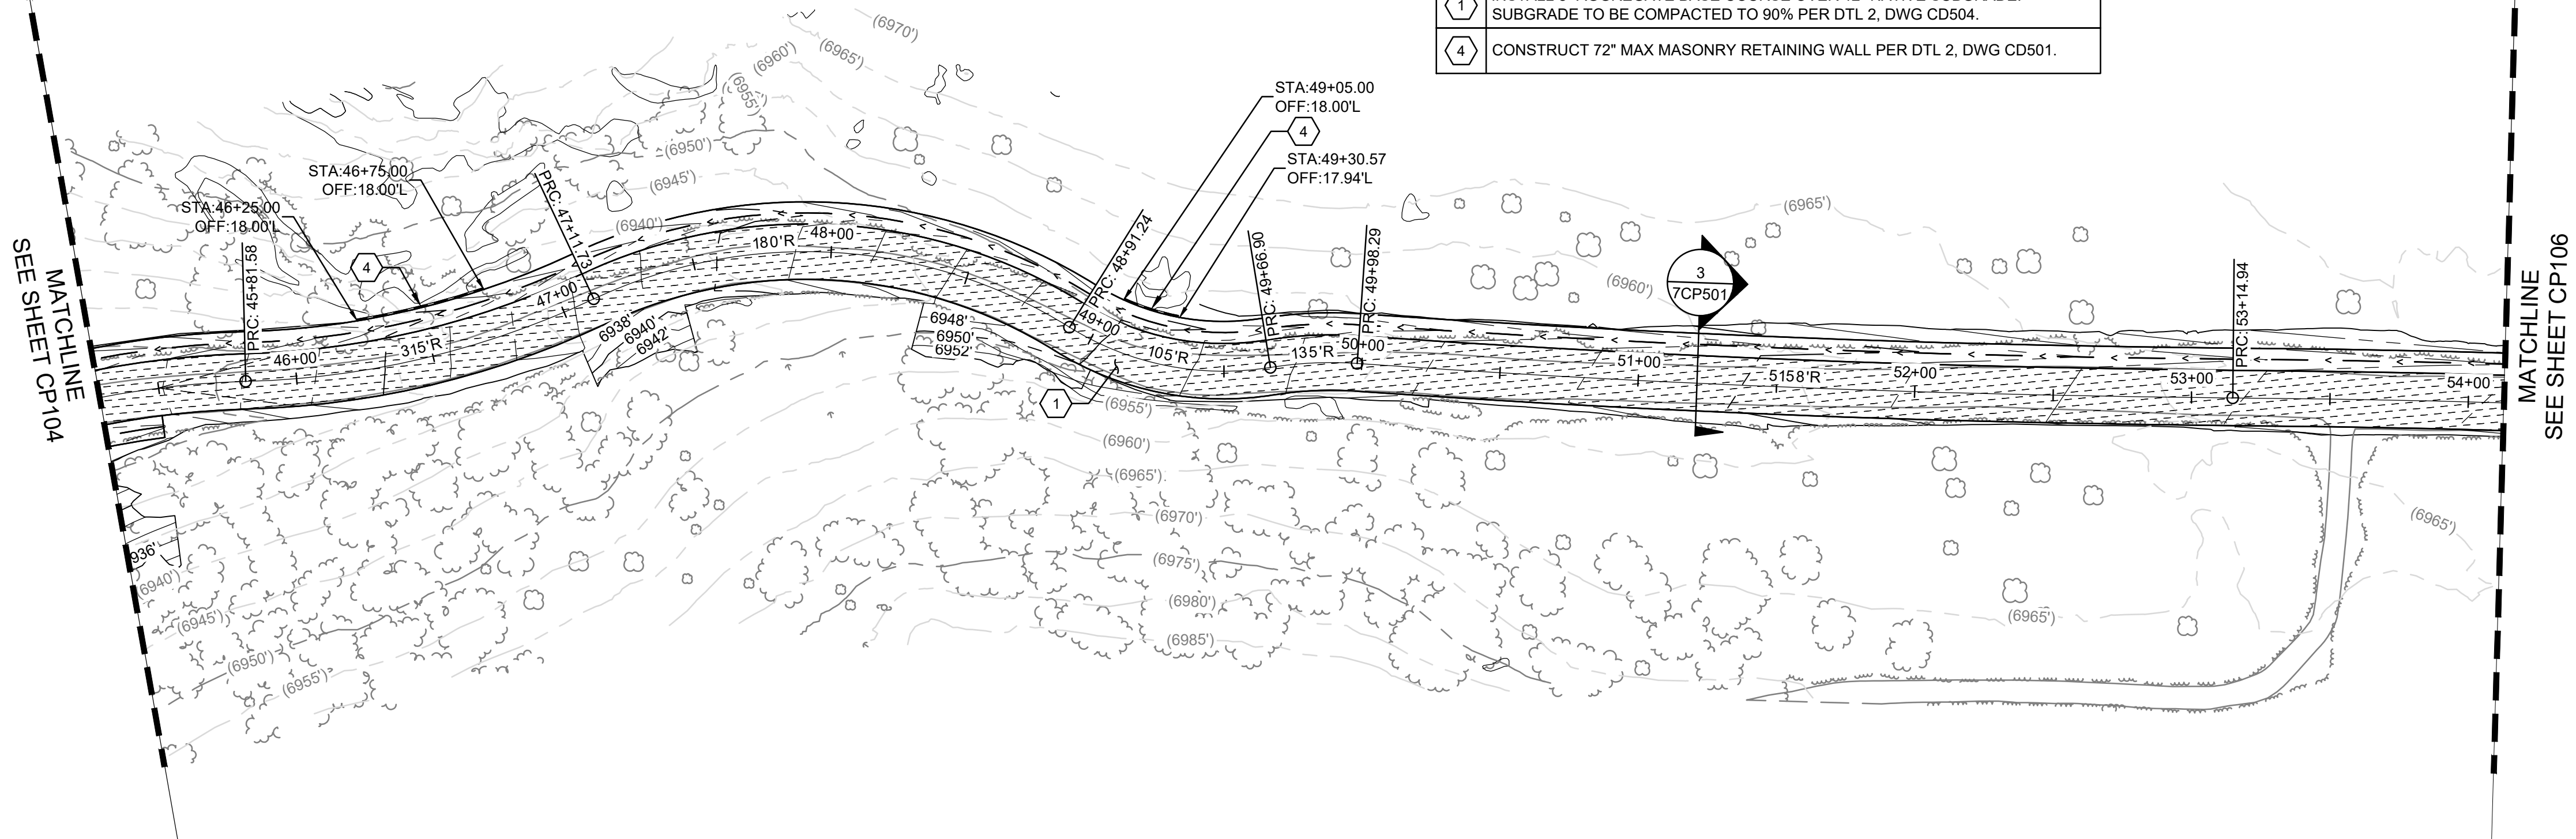

NATIONAL SYSTEM OF PUBLIC LANDS
U.S. DEPARTMENT OF THE INTERIOR
BUREAU OF LAND MANAGEMENT

U.S. DEPARTMENT OF THE INTERIOR
BUREAU OF LAND MANAGEMENT
MARCH 3, 1881

ENGINEER
STATE OF NEVADA
DANIEL F. KELLEY
No. 2114
19 Dec 2025

UNITED STATES DEPARTMENT OF THE INTERIOR
BUREAU OF LAND MANAGEMENT

**GARNET HILL RECREATION AREA TITLE I
AND II SERVICES**

BUREAU OF LAND MANAGEMENT DISTRICT OFFICE
ELY, NEVADA


Project Status
100% CONSTRUCTION DOCUMENTS
BLM Project # 140L0621D0006
Drawn By ABBROWN
Checked By D.KELLEY

Issue Date
12/16/2025


Revision Issue
Description
Rev. #

07 - POLE LINE ROAD
POLE LINE ROAD PLAN &
PROFILE
7CP105

P:\Projects\BLM - NV & CA\IDOT\Task Orders\Task 27 - Garnet Hill Recreation Area\Task 27 - Garnet Hill Recreation Area Title I & II Services\Engineering\Drawings\Production Drawings\07 - ROAD\208-203-07-CP.dwg 12/16/2025 8:16 AM ABBROWN

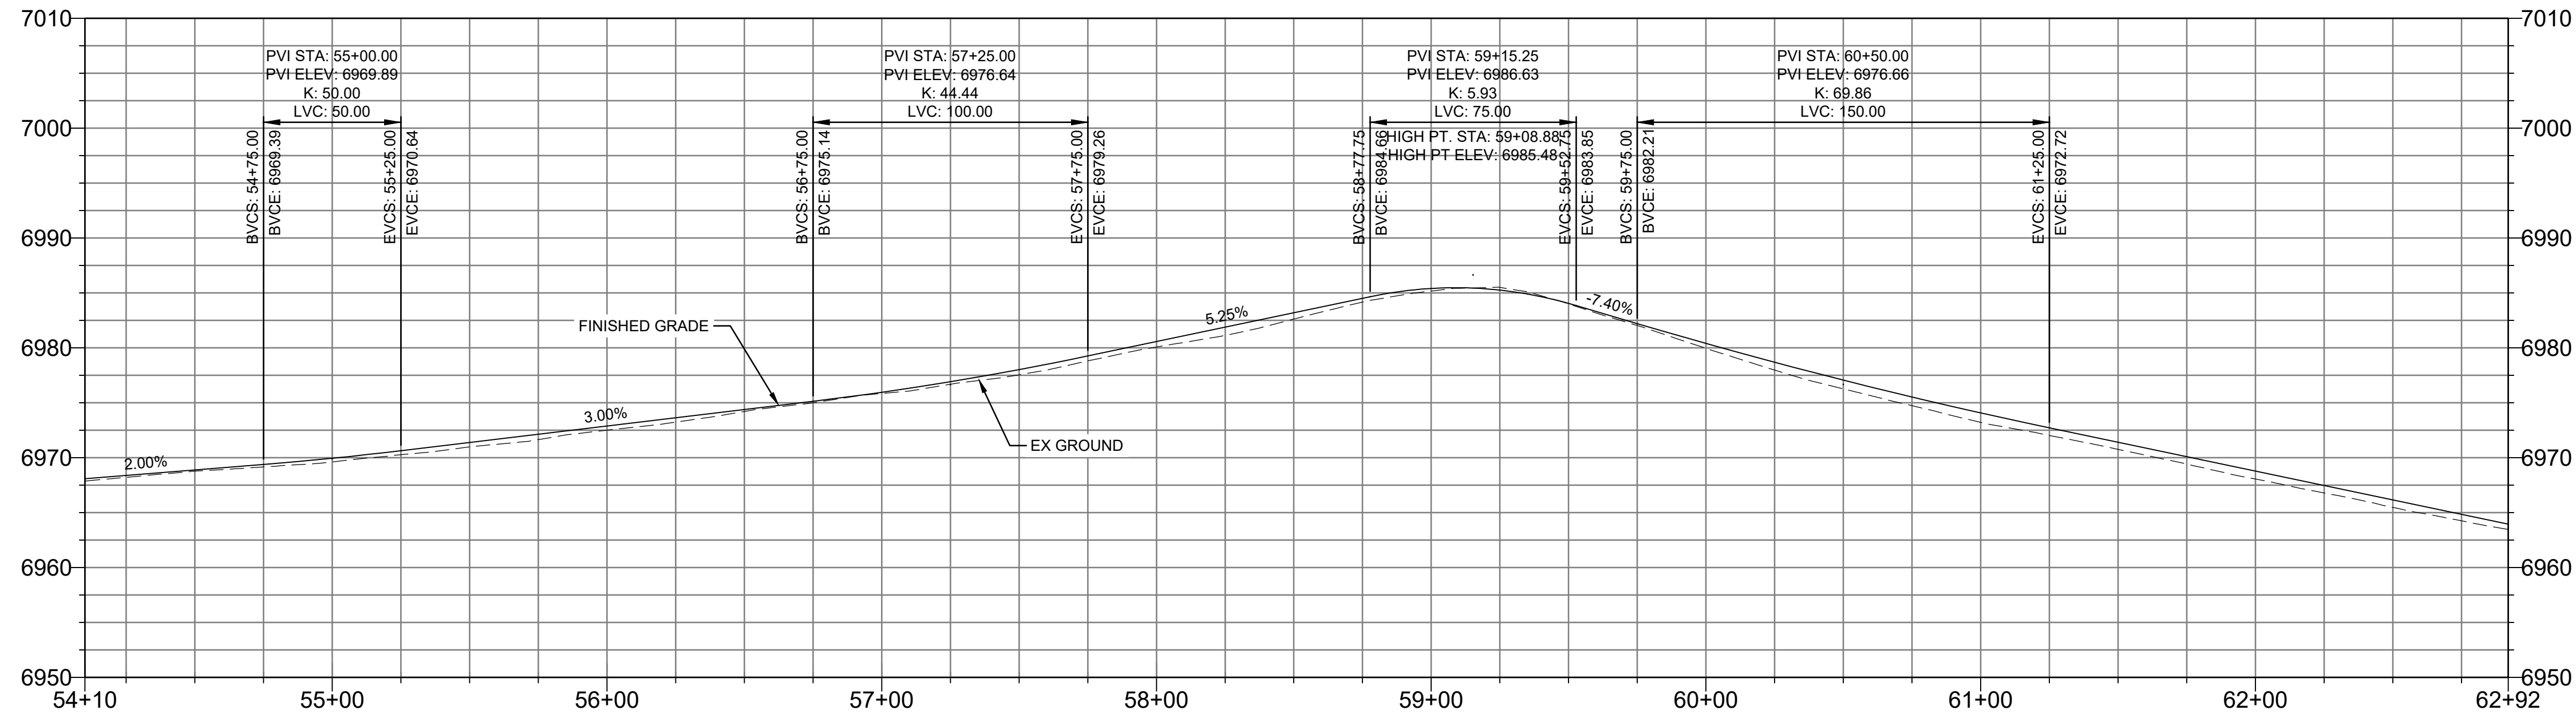

POLE LINE ROAD PLAN & PROFILE
HORIZ: 1" = 40' | VERT: 1" = 4'

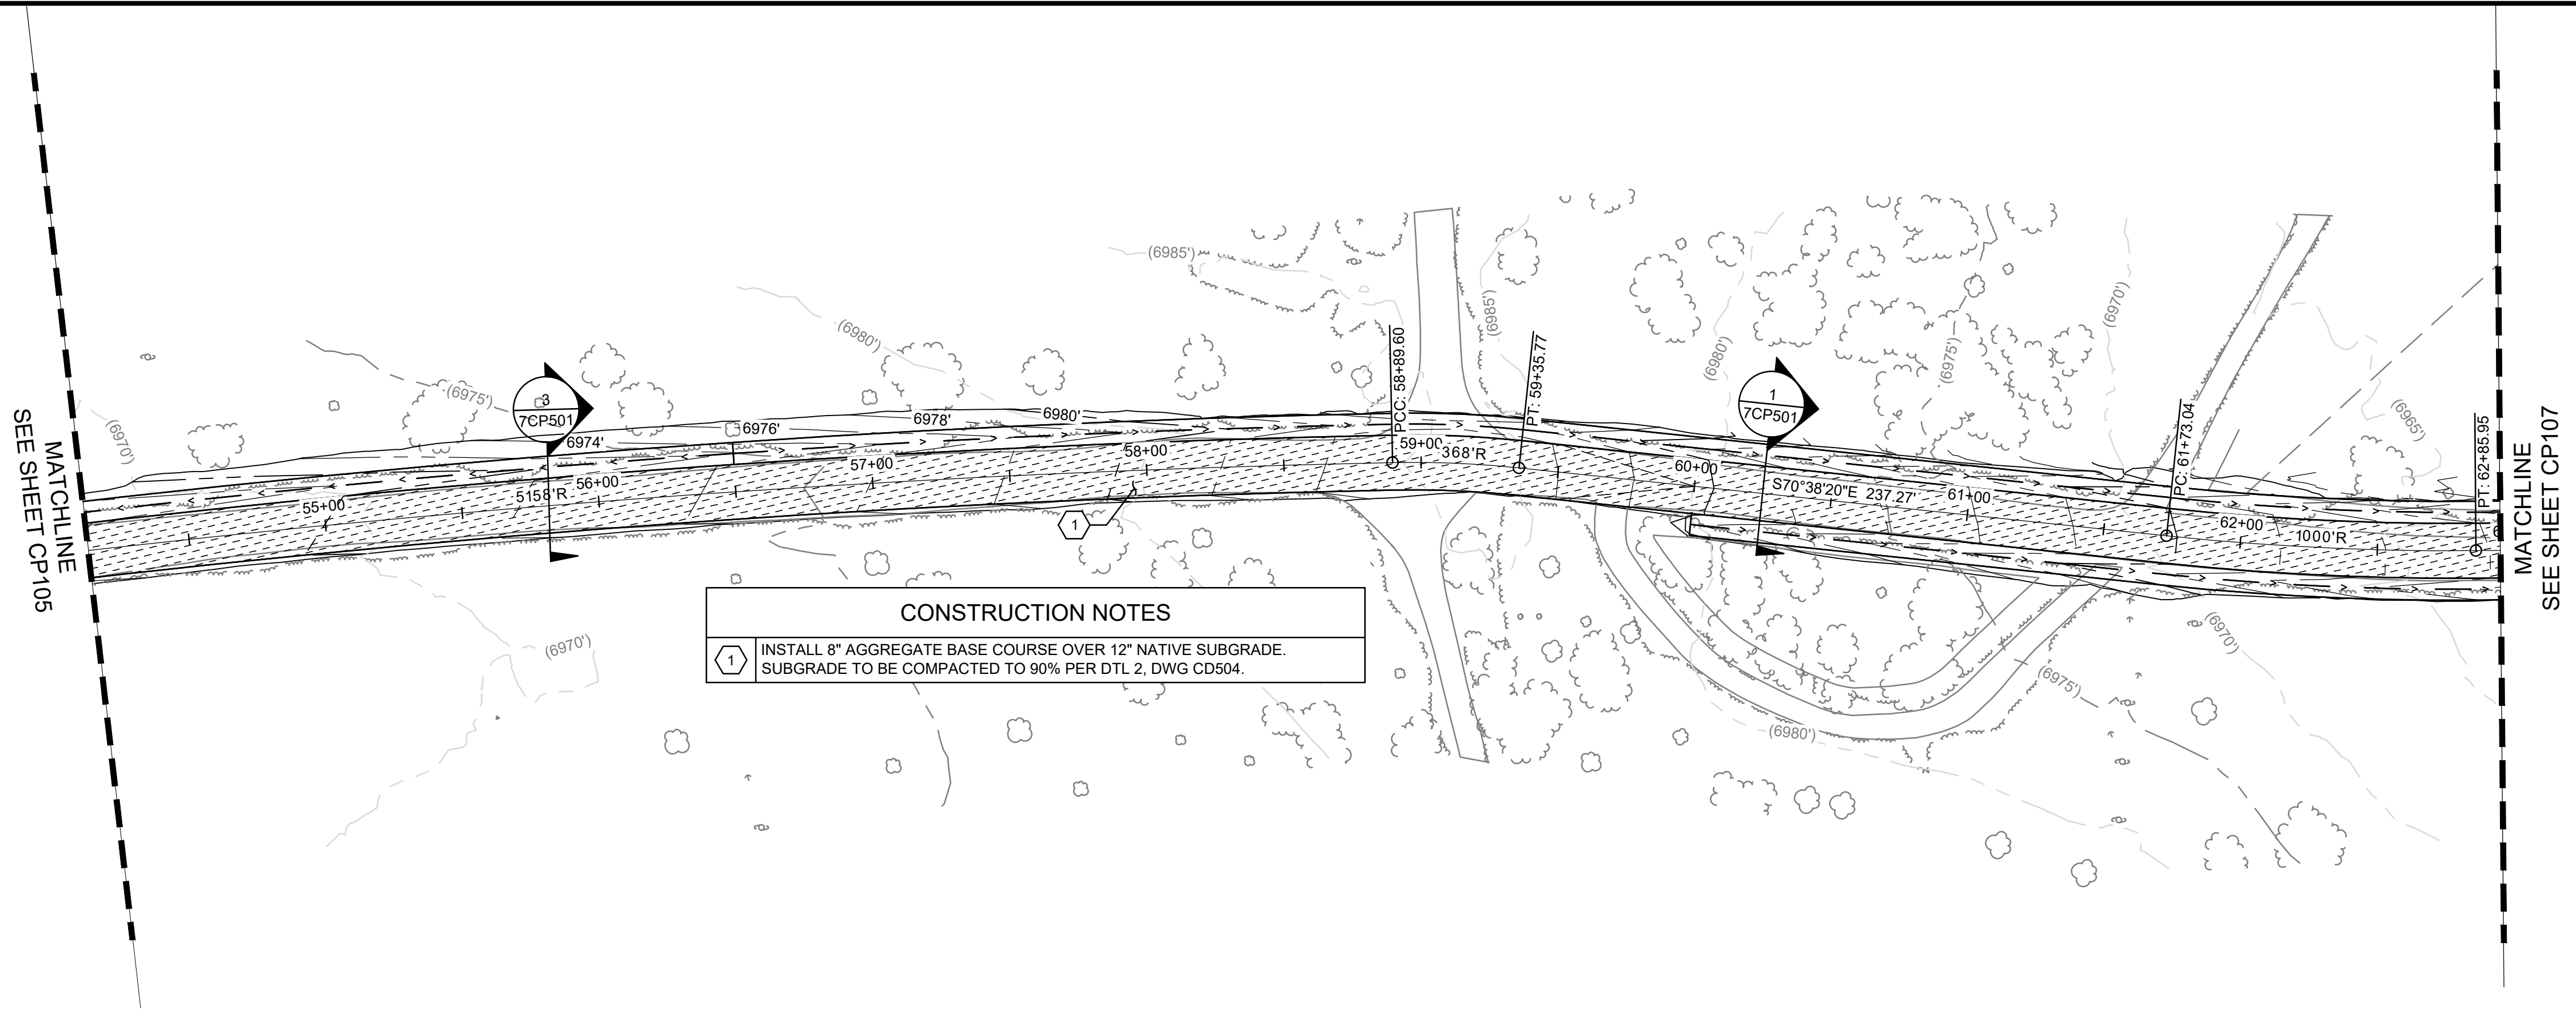

CONSTRUCTION NOTES

1 INSTALL 8" AGGREGATE BASE COURSE OVER 12" NATIVE SUBGRADE.
SUBGRADE TO BE COMPACTED TO 90% PER DTL 2, DWG CD504.

CUT/FILL VOLUMES	
CUT:	1,855 CY
FILL:	4,255 CY
NET:	2,400 CY (FILL)



UNITED STATES DEPARTMENT OF THE INTERIOR
BUREAU OF LAND MANAGEMENT

**GARNET HILL RECREATION AREA TITLE I
AND II SERVICES**

BUREAU OF LAND MANAGEMENT DISTRICT OFFICE
ELY, NEVADA



Project Status	Issue Date
100% CONSTRUCTION DOCUMENTS	12/16/2025
BLM Project #	140L0621D0006
Drawn By	ABBROWN
Checked By	D.KELLEY

07 - POLE LINE ROAD
POLE LINE ROAD PLAN &
PROFILE


7CP106

19 Dec 2025

P:\Projects\BLM - NV & CA ID\Task Orders\Task 27 - Garnet Hill Recreation Area\Task 27 - I Services\Engineering\Drawings\Production Drawings\07 - ROAD\208-203-07-CP.dwg 12/16/2025 8:16 AM A.BROWN

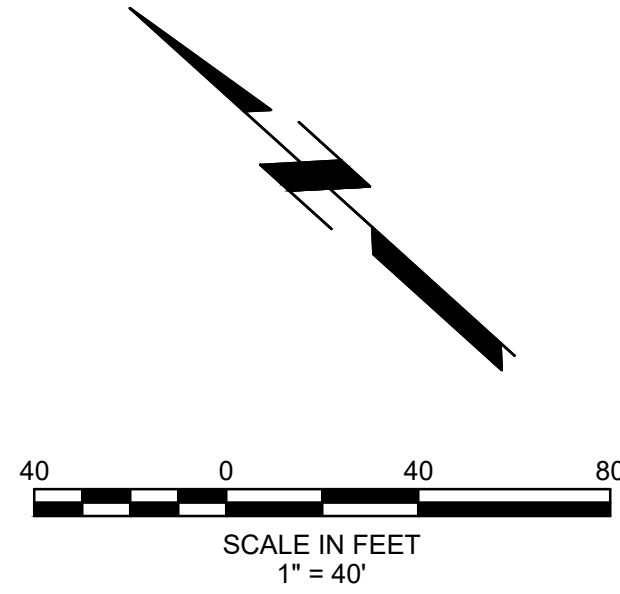
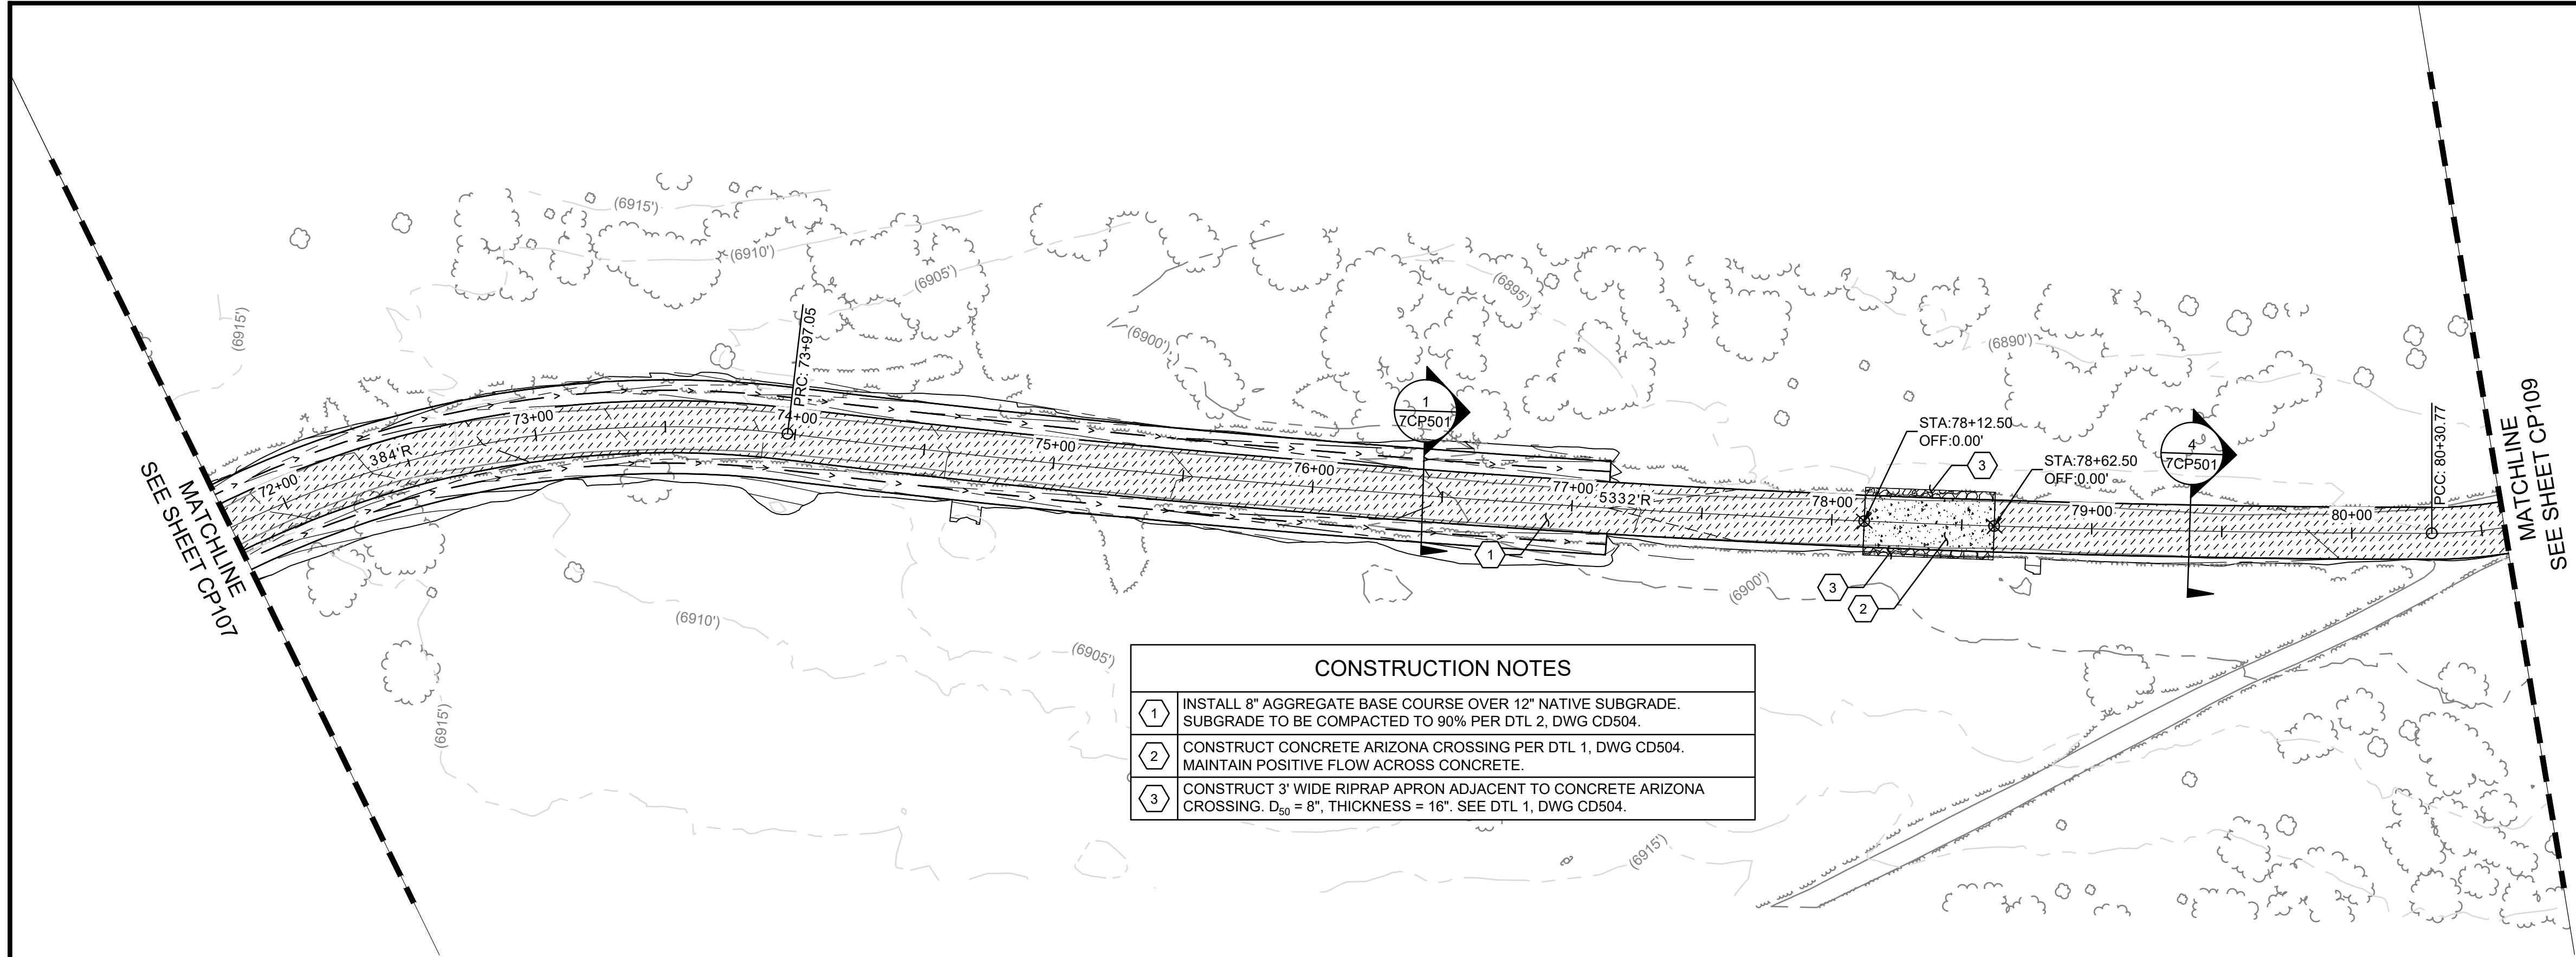


CUT/FILL VOLUMES	
CUT:	1,855 CY
FILL:	4,255 CY
NET:	2,400 CY (FILL)

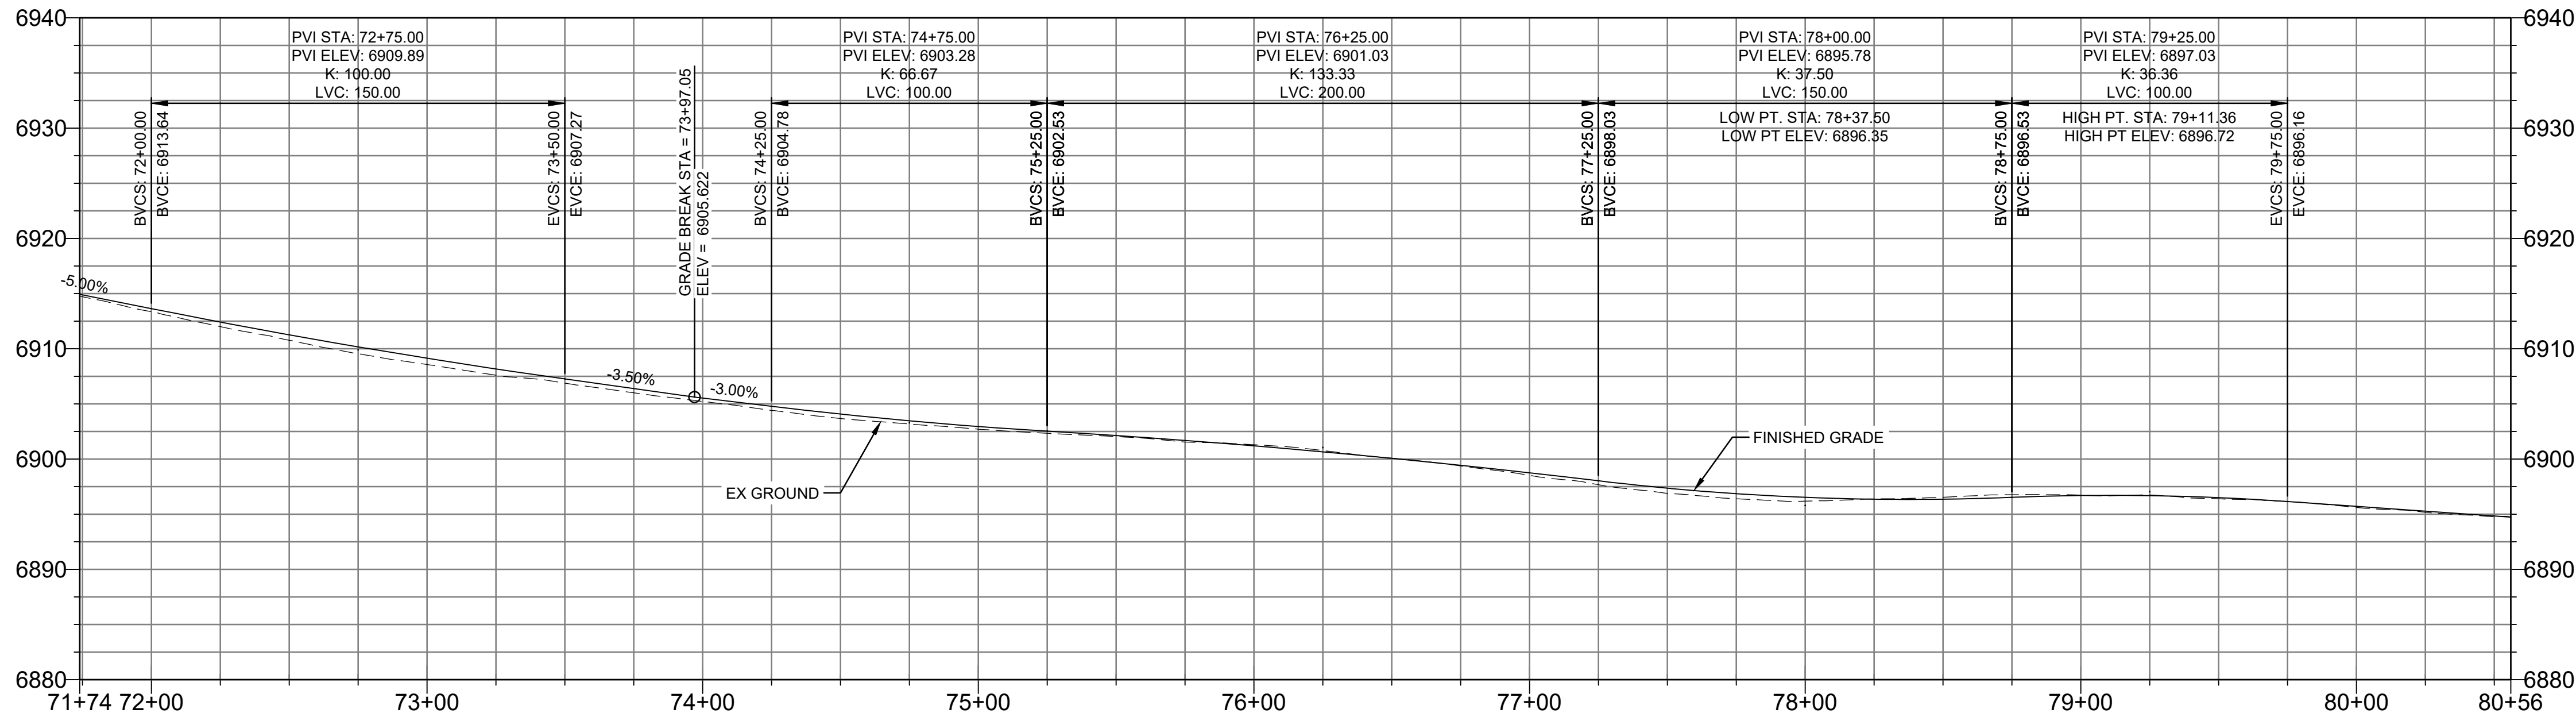

POLE LINE ROAD PLAN & PROFILE
HORIZ: 1" = 40' | VERT: 1" = 4'

1
7CP108

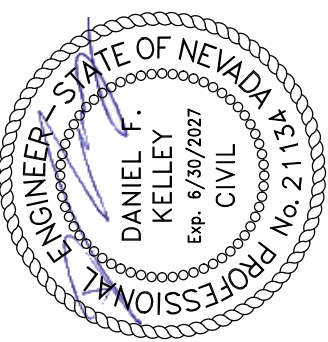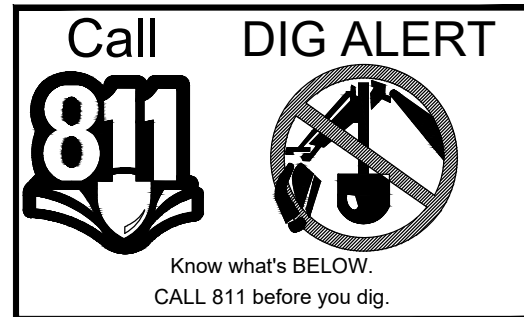

UNITED STATES DEPARTMENT OF THE INTERIOR
BUREAU OF LAND MANAGEMENT

GARNET HILL RECREATION AREA TITLE I AND II SERVICES

BUREAU OF LAND MANAGEMENT DISTRICT OFFICE
ELY, NEVADA



Project Status	Issue Date
100% CONSTRUCTION DOCUMENTS	12/16/2025
BLM Project #	140L0621D0006
Drawn By	A.BROWN
Checked By	D.KELLEY

Revision Issue	Date
Description	
Rev. #	


07 - POLE LINE ROAD
POLE LINE ROAD PLAN &
PROFILE
7CP108

19 Dec 2025

P:\Projects\BLM - NV & CA\IDOTask Orders\Task 27 - Garnet Hill Recreation Area\Task 27 - Garnet Hill Recreation Area Title I & II Services\Engineering\Drawings\Production Drawings\07 - ROAD\208-203-07-CP.dwg 12/16/2025 8:16 AM ABBROWN

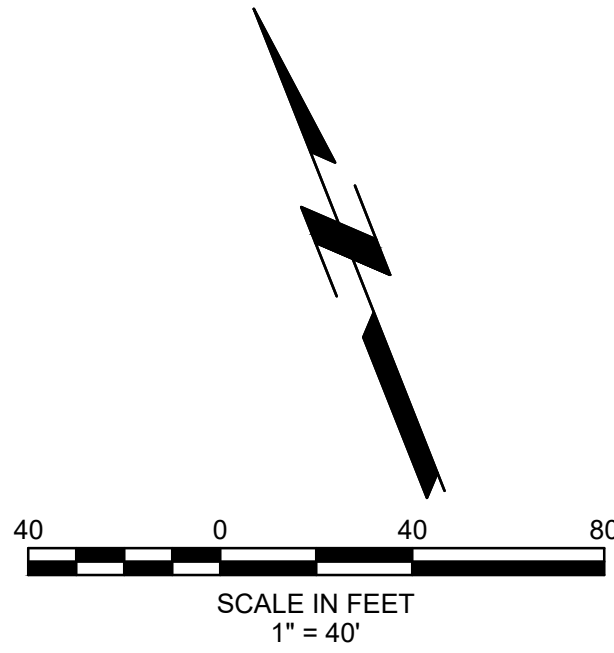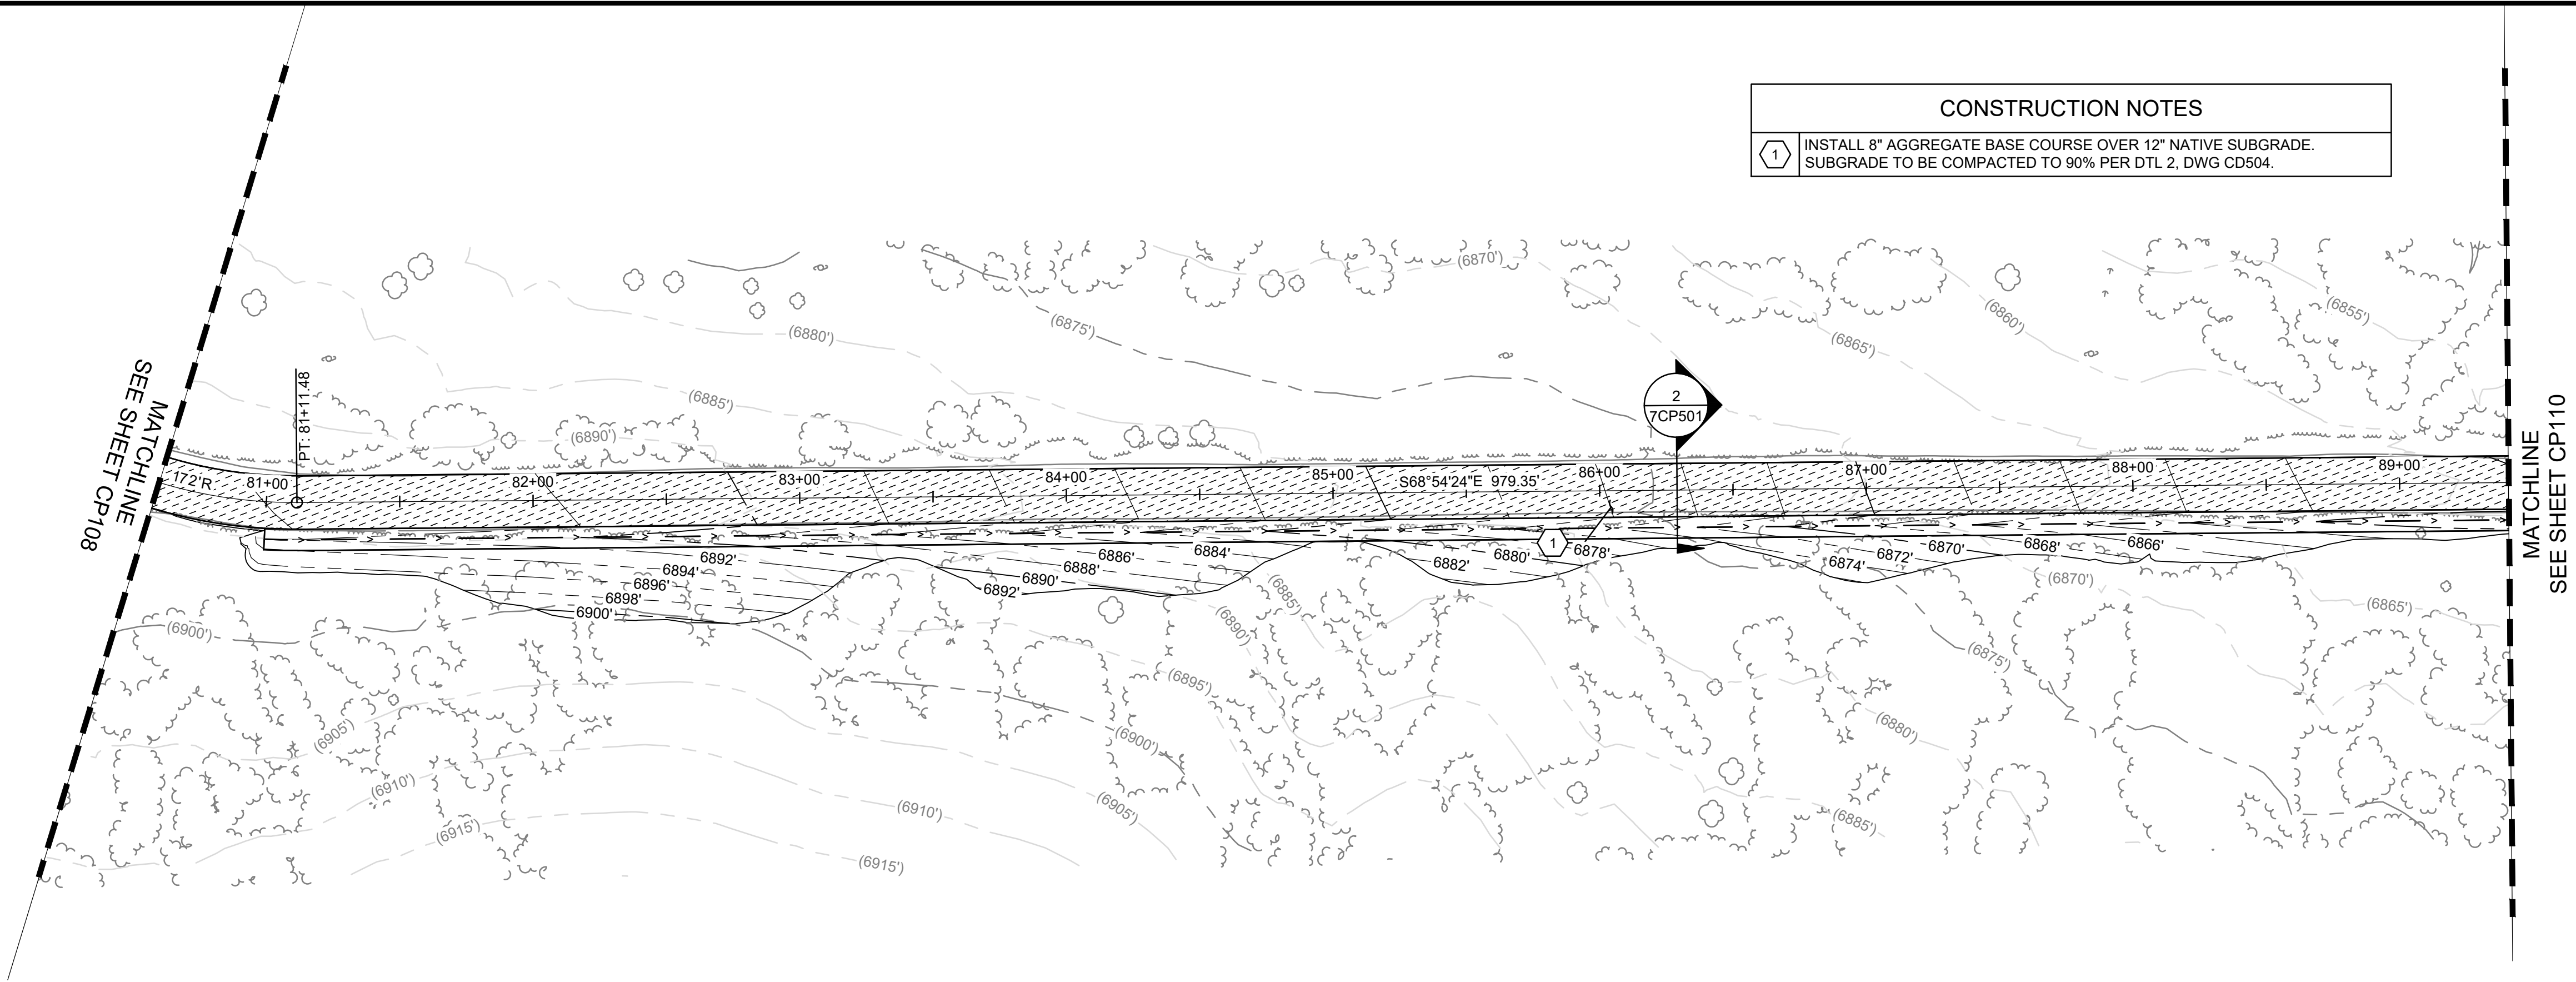



CUT/FILL VOLUMES	
CUT:	1,855 CY
FILL:	4,255 CY
NET:	2,400 CY (FILL)

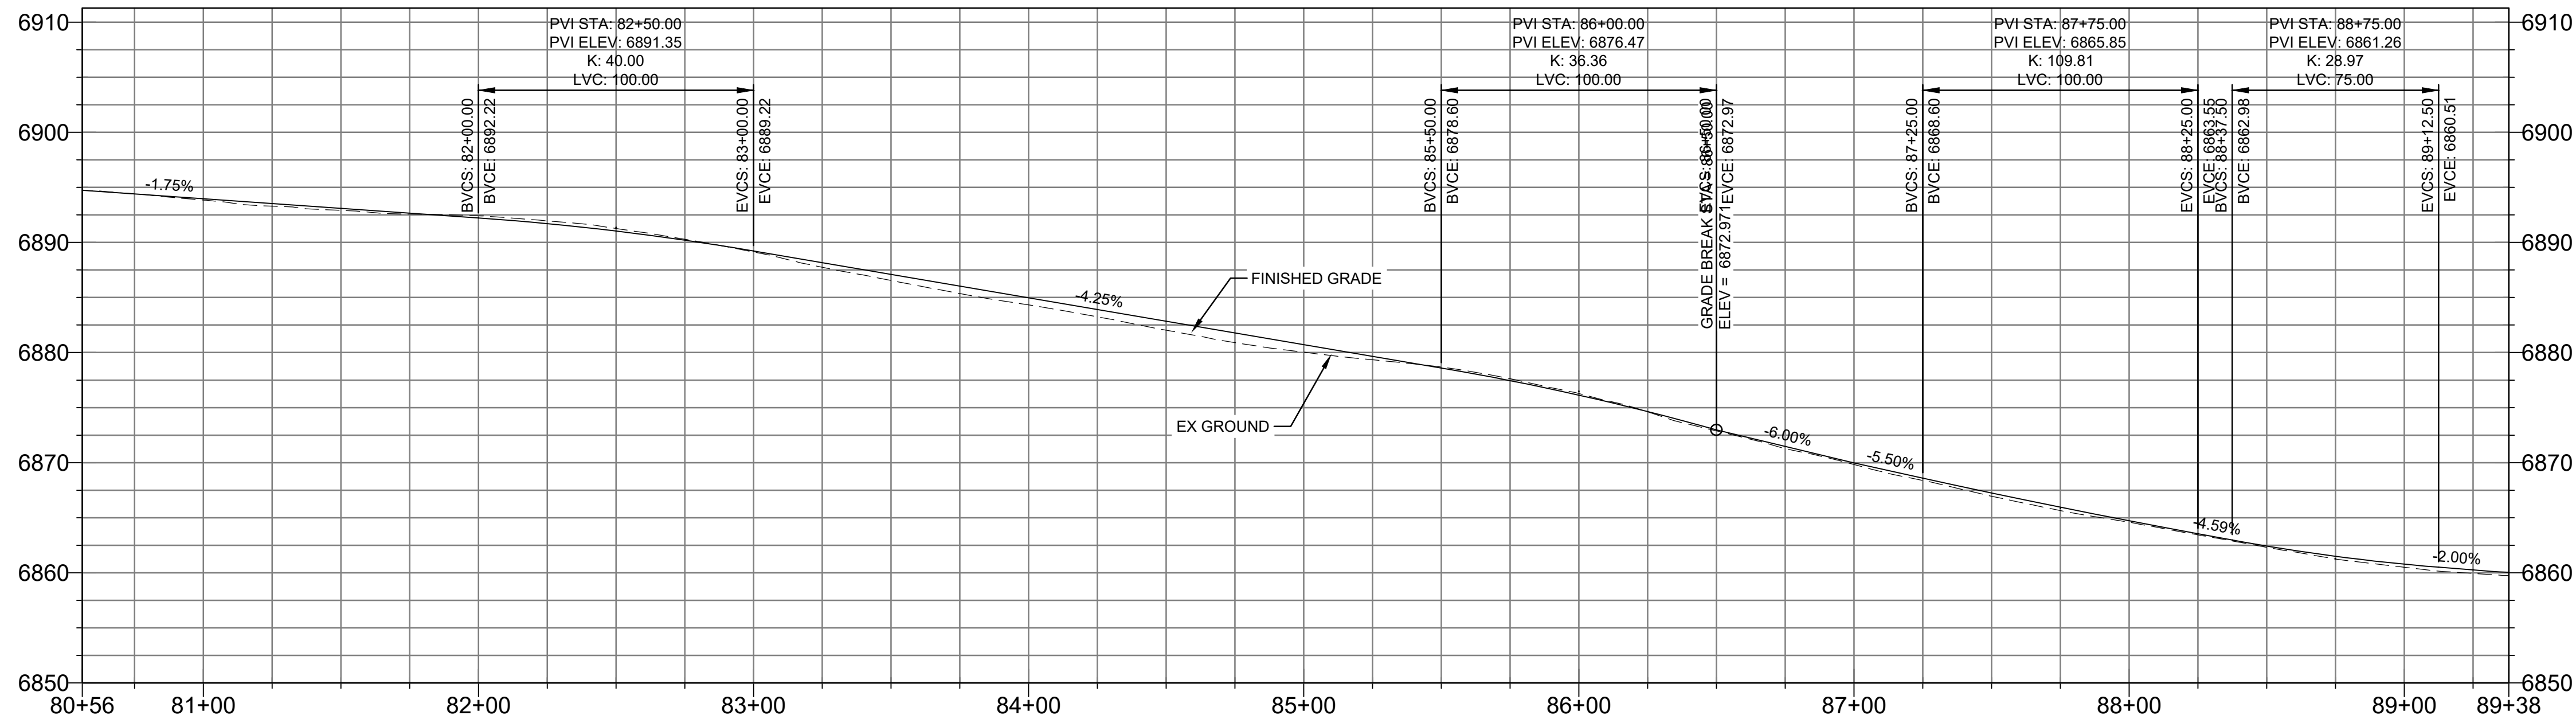

POLE LINE ROAD PLAN & PROFILE

HORIZ: 1" = 40' | VERT: 1" = 4'

1
7CP109

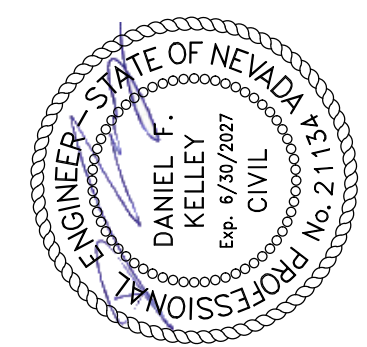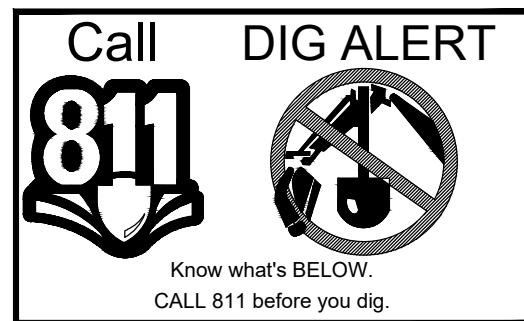

UNITED STATES DEPARTMENT OF THE INTERIOR
BUREAU OF LAND MANAGEMENT

**GARNET HILL RECREATION AREA TITLE I
AND II SERVICES**

BUREAU OF LAND MANAGEMENT DISTRICT OFFICE
ELY, NEVADA

Revision Issue	Date	Description	Rev. #
Project Status	100%	CONSTRUCTION DOCUMENTS	
Issue Date	12/16/2025		
BLM Project #	140L0621D0006		
Drawn By	ABBROWN		
Checked By	D.KELLEY		


07 - POLE LINE ROAD
POLE LINE ROAD PLAN &
PROFILE

7CP109


19 Dec 2025



P:\Projects\BLM - NV & CA IDIO\Task Orders\Task 27 - Garnet Hill Recreation Area\Task 27 - Garnet Hill Recreation Area Title I & II Services\Engineering\Drawings\Production Drawings\07 - ROAD\208-203-07-CP.dwg 12/16/2025 8:16 AM ABBROWN

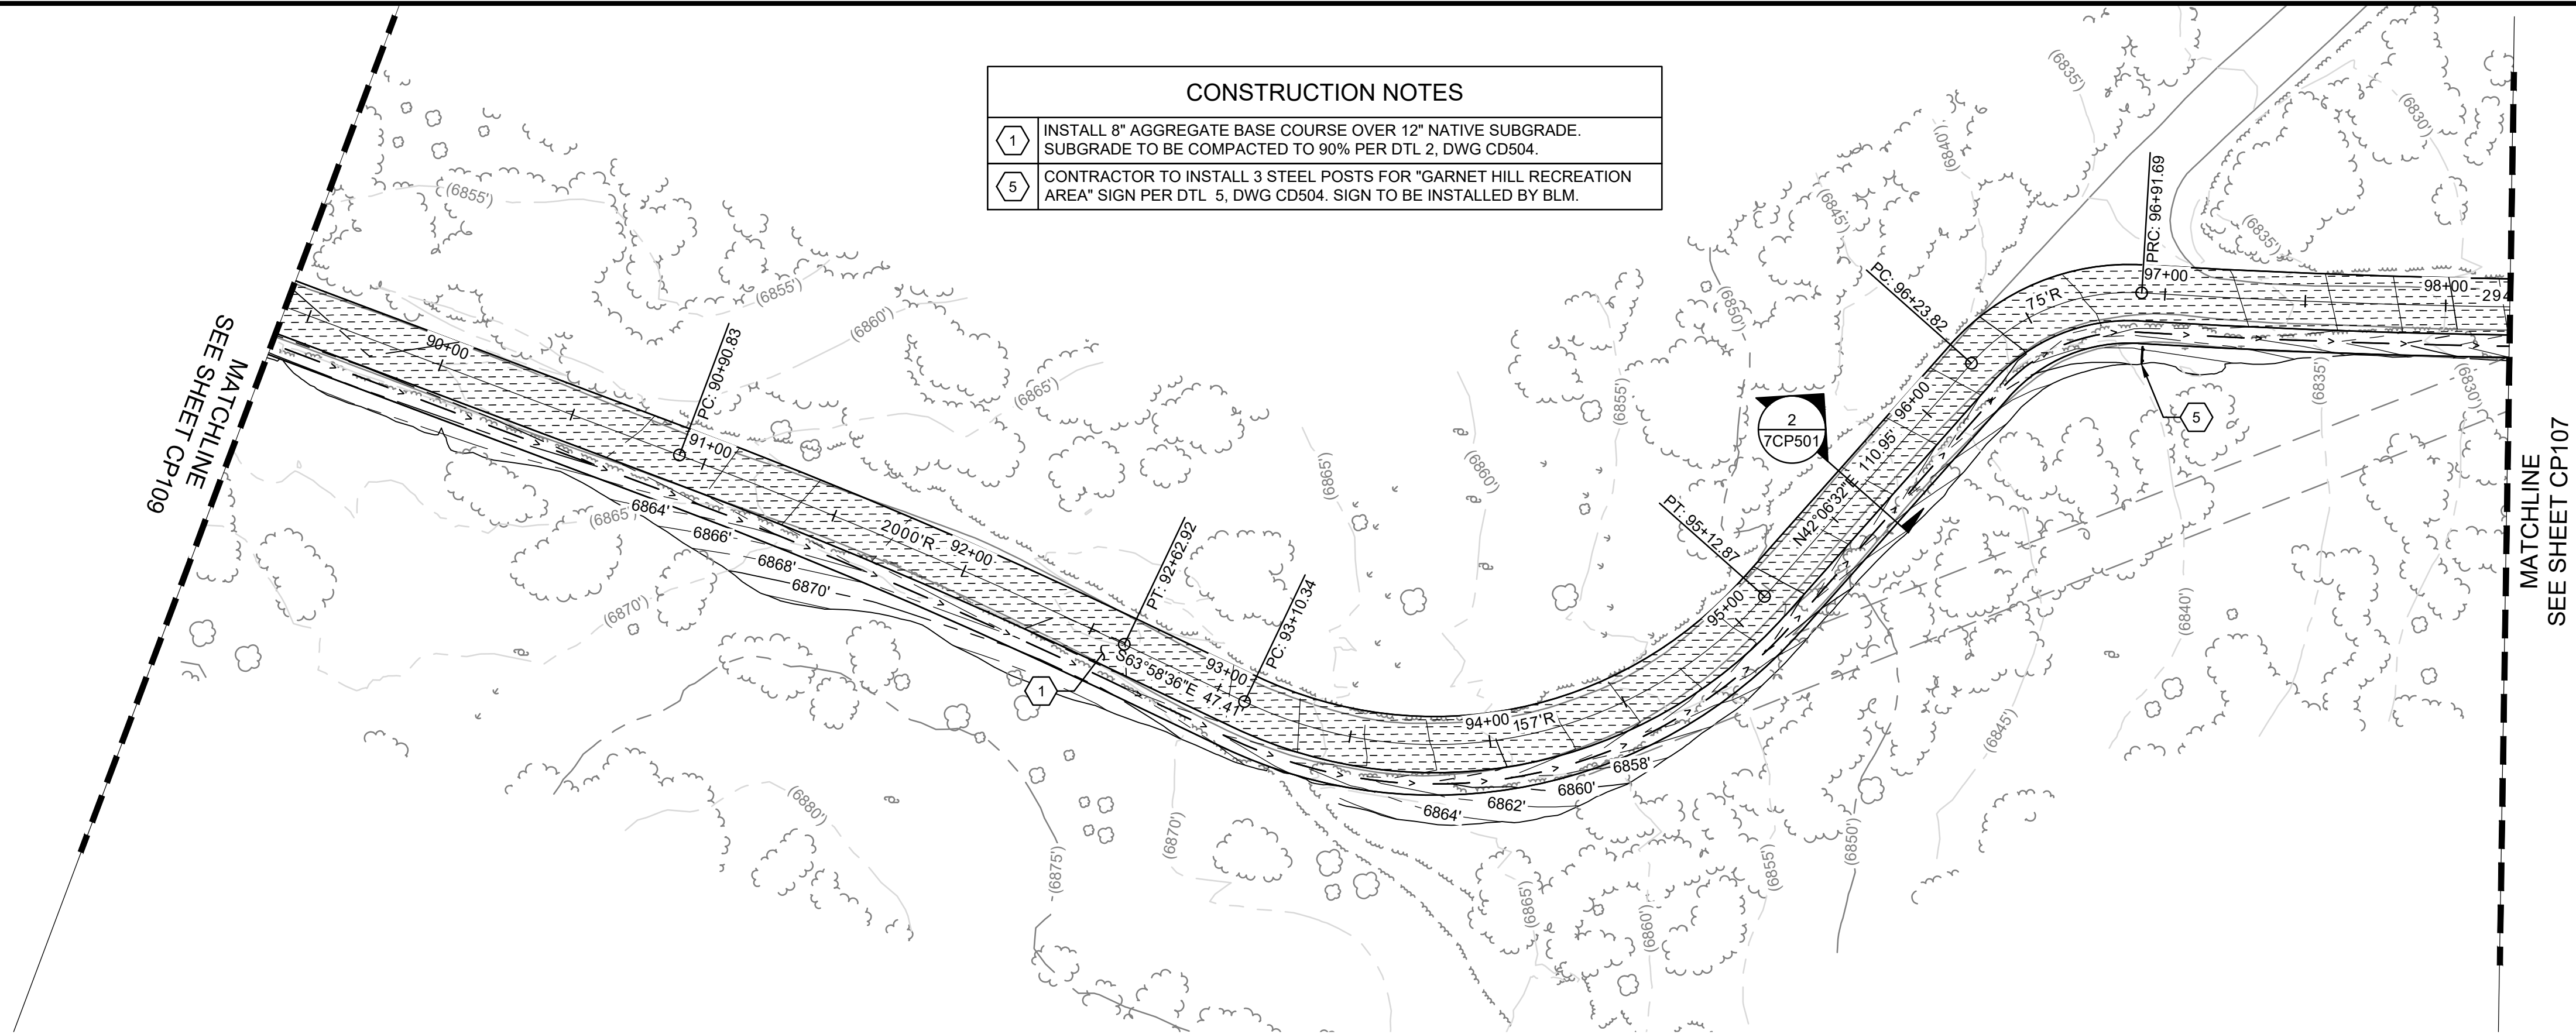

CUT/FILL VOLUMES	
CUT:	1,855 CY
FILL:	4,255 CY
NET:	2,400 CY (FILL)

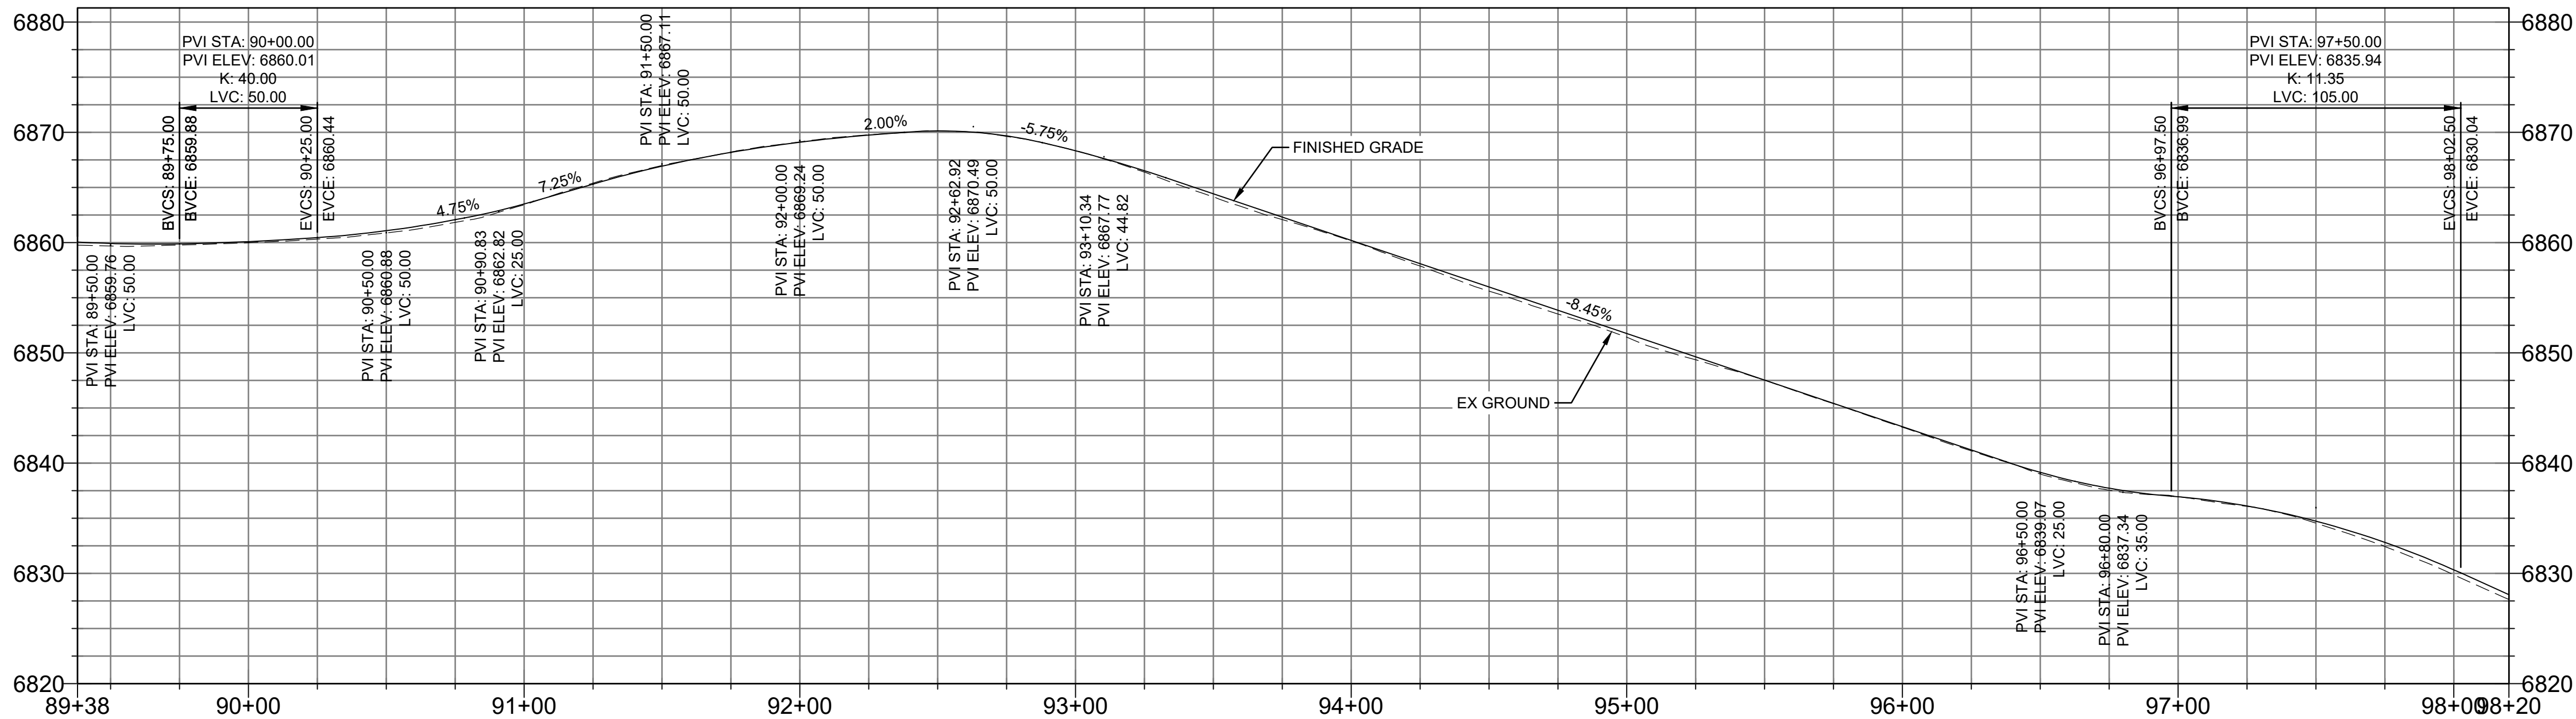

UNITED STATES DEPARTMENT OF THE INTERIOR
BUREAU OF LAND MANAGEMENT

GARNET HILL RECREATION AREA TITLE I AND II SERVICES

BUREAU OF LAND MANAGEMENT DISTRICT OFFICE
ELY, NEVADA


Project Status	Issue Date
100% CONSTRUCTION DOCUMENTS	12/16/2025
BLM Project #	140L0621D0006
Drawn By	ABBROWN
Checked By	D.KELLEY

Revision	Issue	Date
Rev. #	Description	

07 - POLE LINE ROAD
POLE LINE ROAD PLAN &
PROFILE

7CP110

P:\Projects\BLM - NV & CA\IDOT\Task Orders\Task 27 - Garnet Hill Recreation Area\Task 27 - Garnet Hill Recreation Area Title I & II Services\Engineering\Drawings\Production Drawings\07 - ROAD\208-203-07-CP.dwg 12/16/2025 8:16 AM A.BROWN

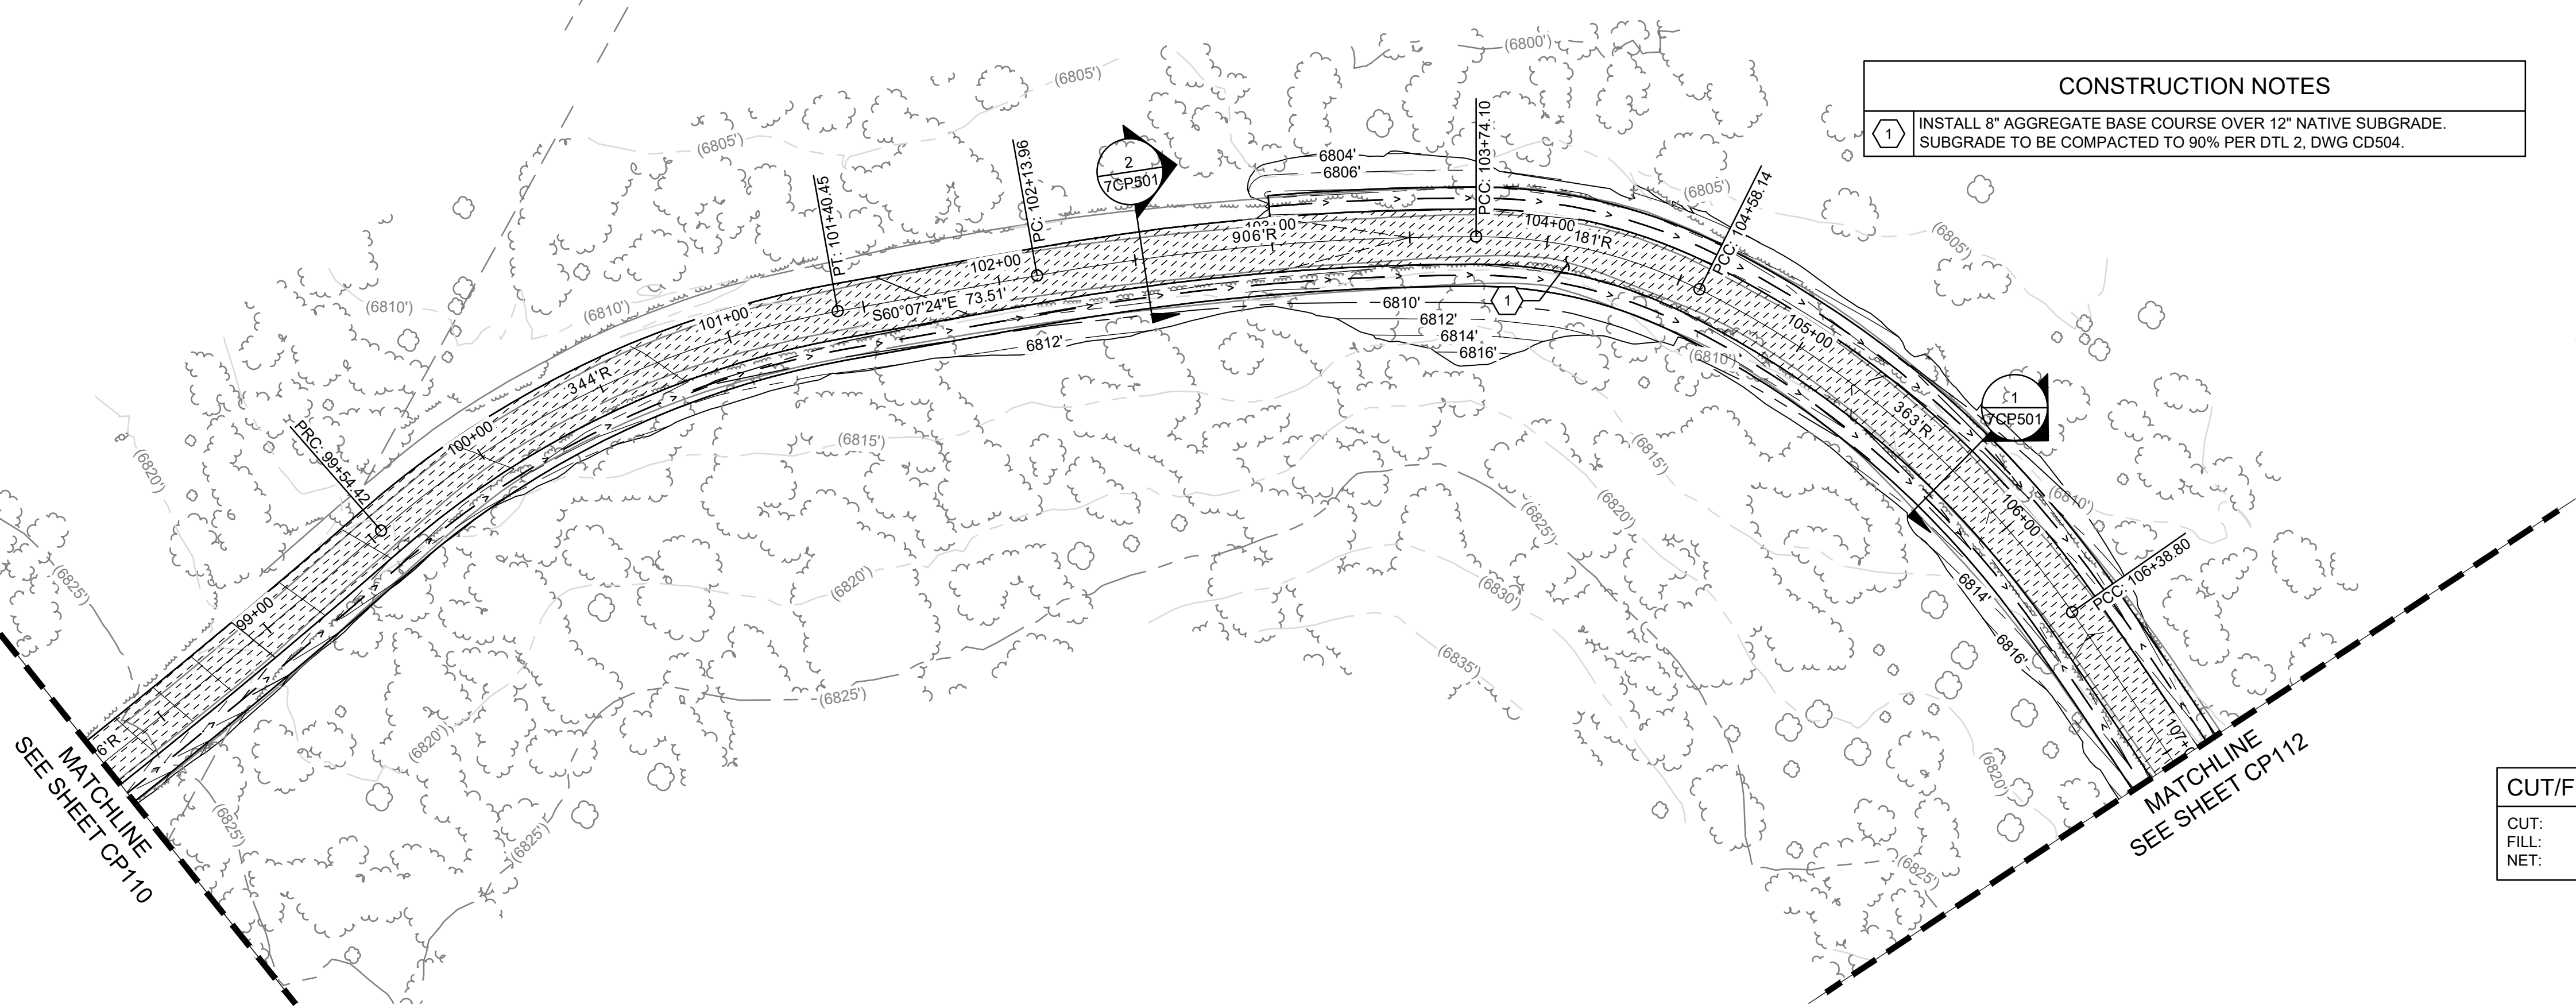


CONSTRUCTION NOTES

1. INSTALL 8" AGGREGATE BASE COURSE OVER 12" NATIVE SUBGRADE. SUBGRADE TO BE COMPACTED TO 90% PER DTL 2, DWG CD504.

SCALE IN FEET
1" = 40'

CUT/FILL VOLUMES

CUT: 1,855 CY
FILL: 4,255 CY
NET: 2,400 CY (FILL)

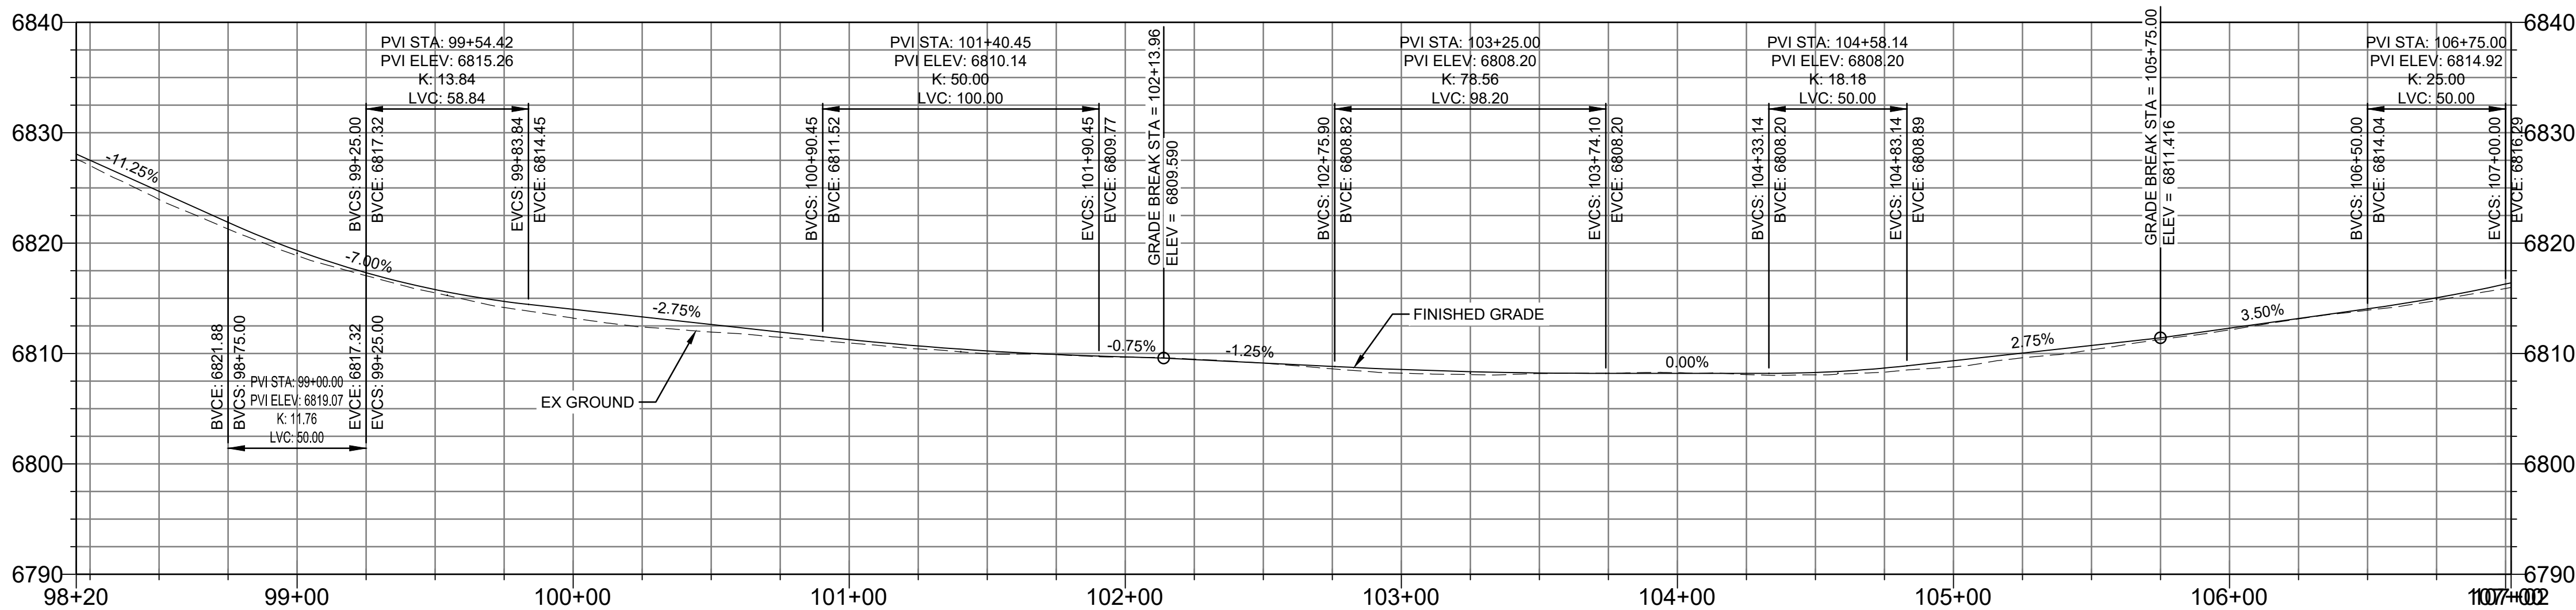

POLE LINE ROAD PLAN & PROFILE
HORIZ: 1" = 40' | VERT: 1" = 4'

1
7CP111



UNITED STATES DEPARTMENT OF THE INTERIOR
BUREAU OF LAND MANAGEMENT

**GARNET HILL RECREATION AREA TITLE I
AND II SERVICES**

BUREAU OF LAND MANAGEMENT DISTRICT OFFICE
ELY, NEVADA

Issue Date
12/16/2025

Project Status
100% CONSTRUCTION DOCUMENTS

BLM Project #
140L0621D0006


Drawn By
A.BROWN

Checked By
D.KELLEY


07 - POLE LINE ROAD
POLE LINE ROAD PLAN &
PROFILE

7CP111

P:\Projects\BLM - NV & CA\IDOT\Task Orders\Task 27 - Garnet Hill Recreation Area\Task 1 & I Services\Engineering\Drawings\Production Drawings\07 - ROAD\208-203-07-CP.dwg 12/16/2025 8:16 AM A.BROWN

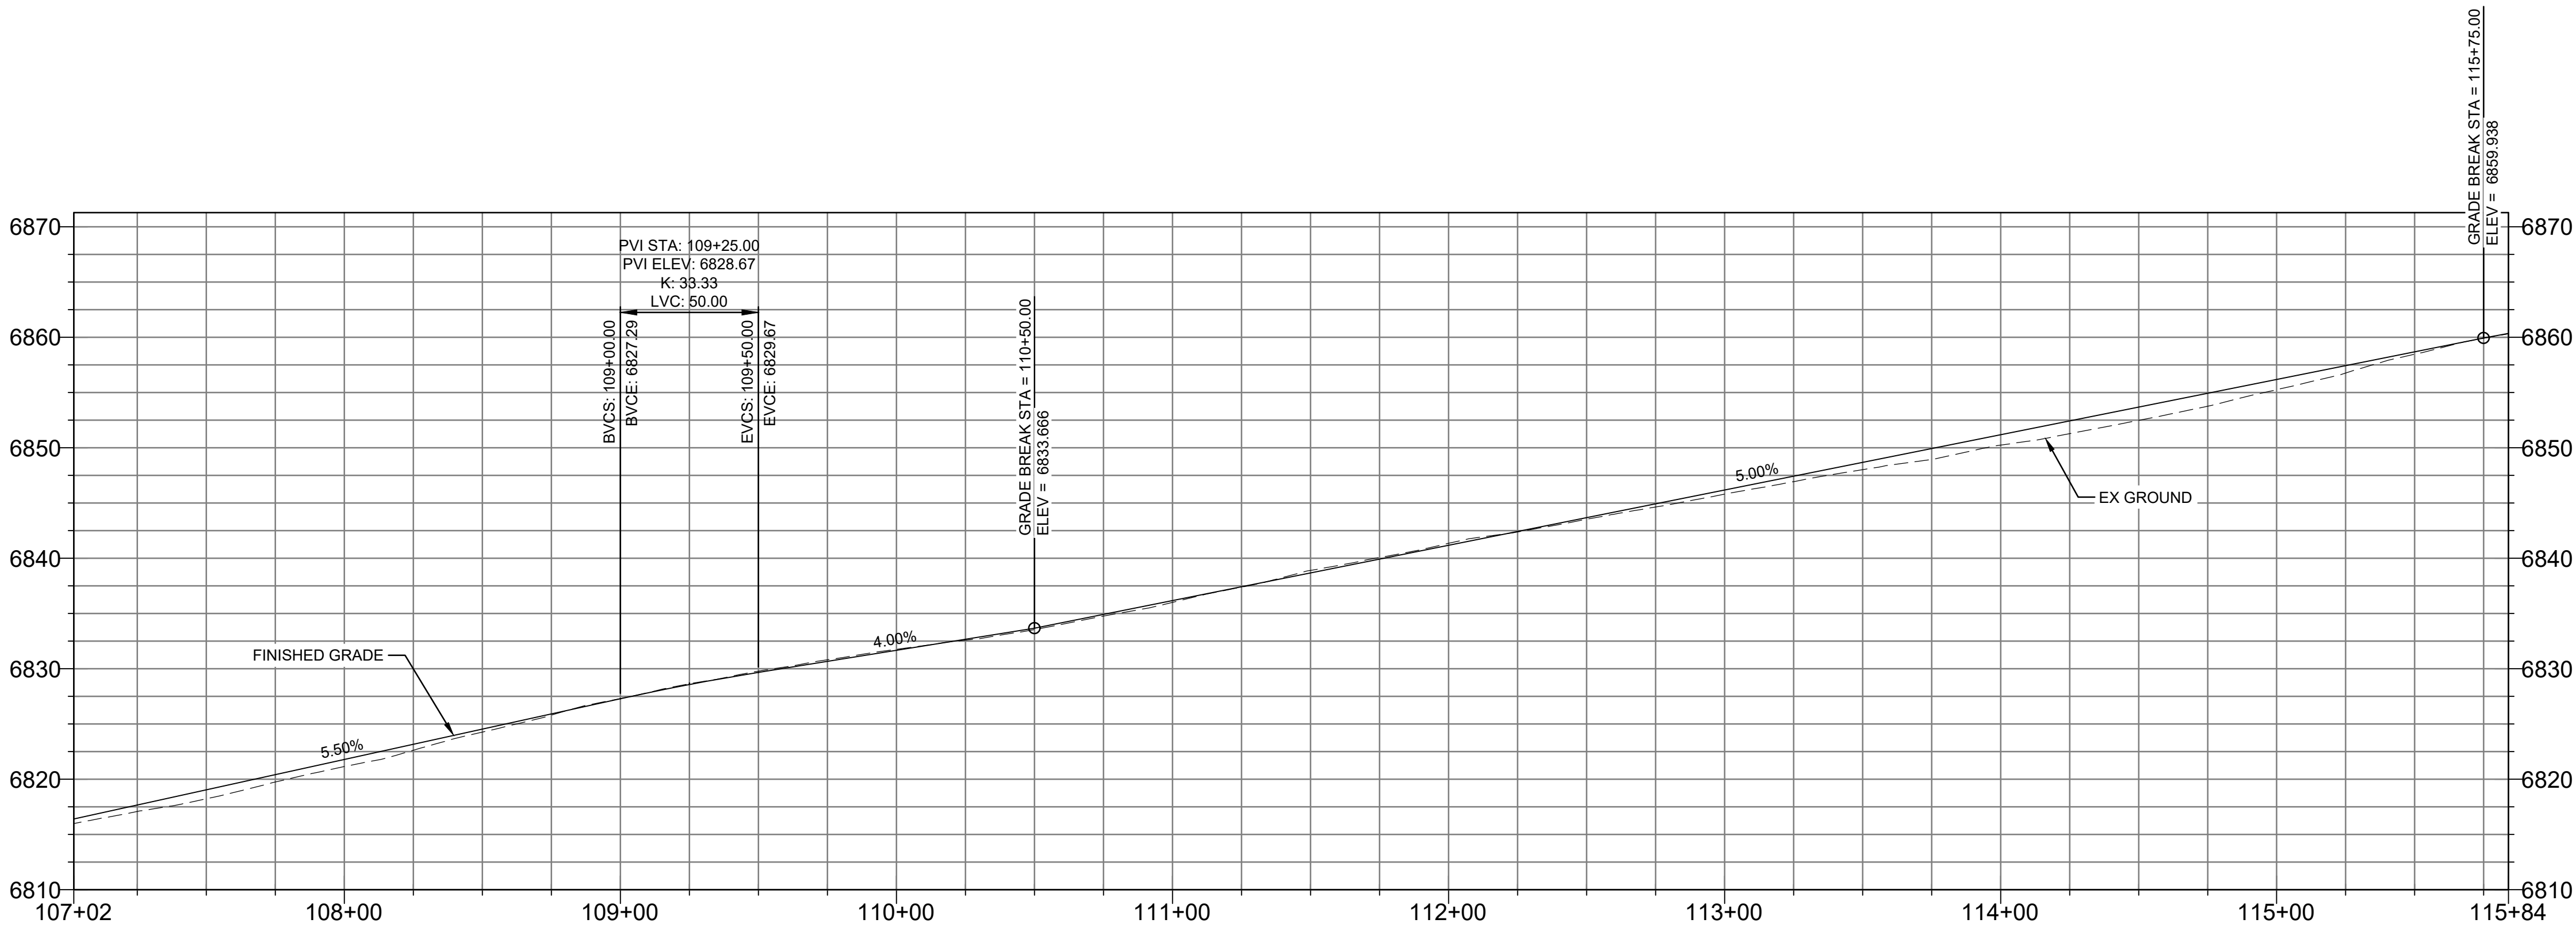

POLE LINE ROAD PLAN & PROFILE
HORIZ: 1" = 40' | VERT: 1" = 4'

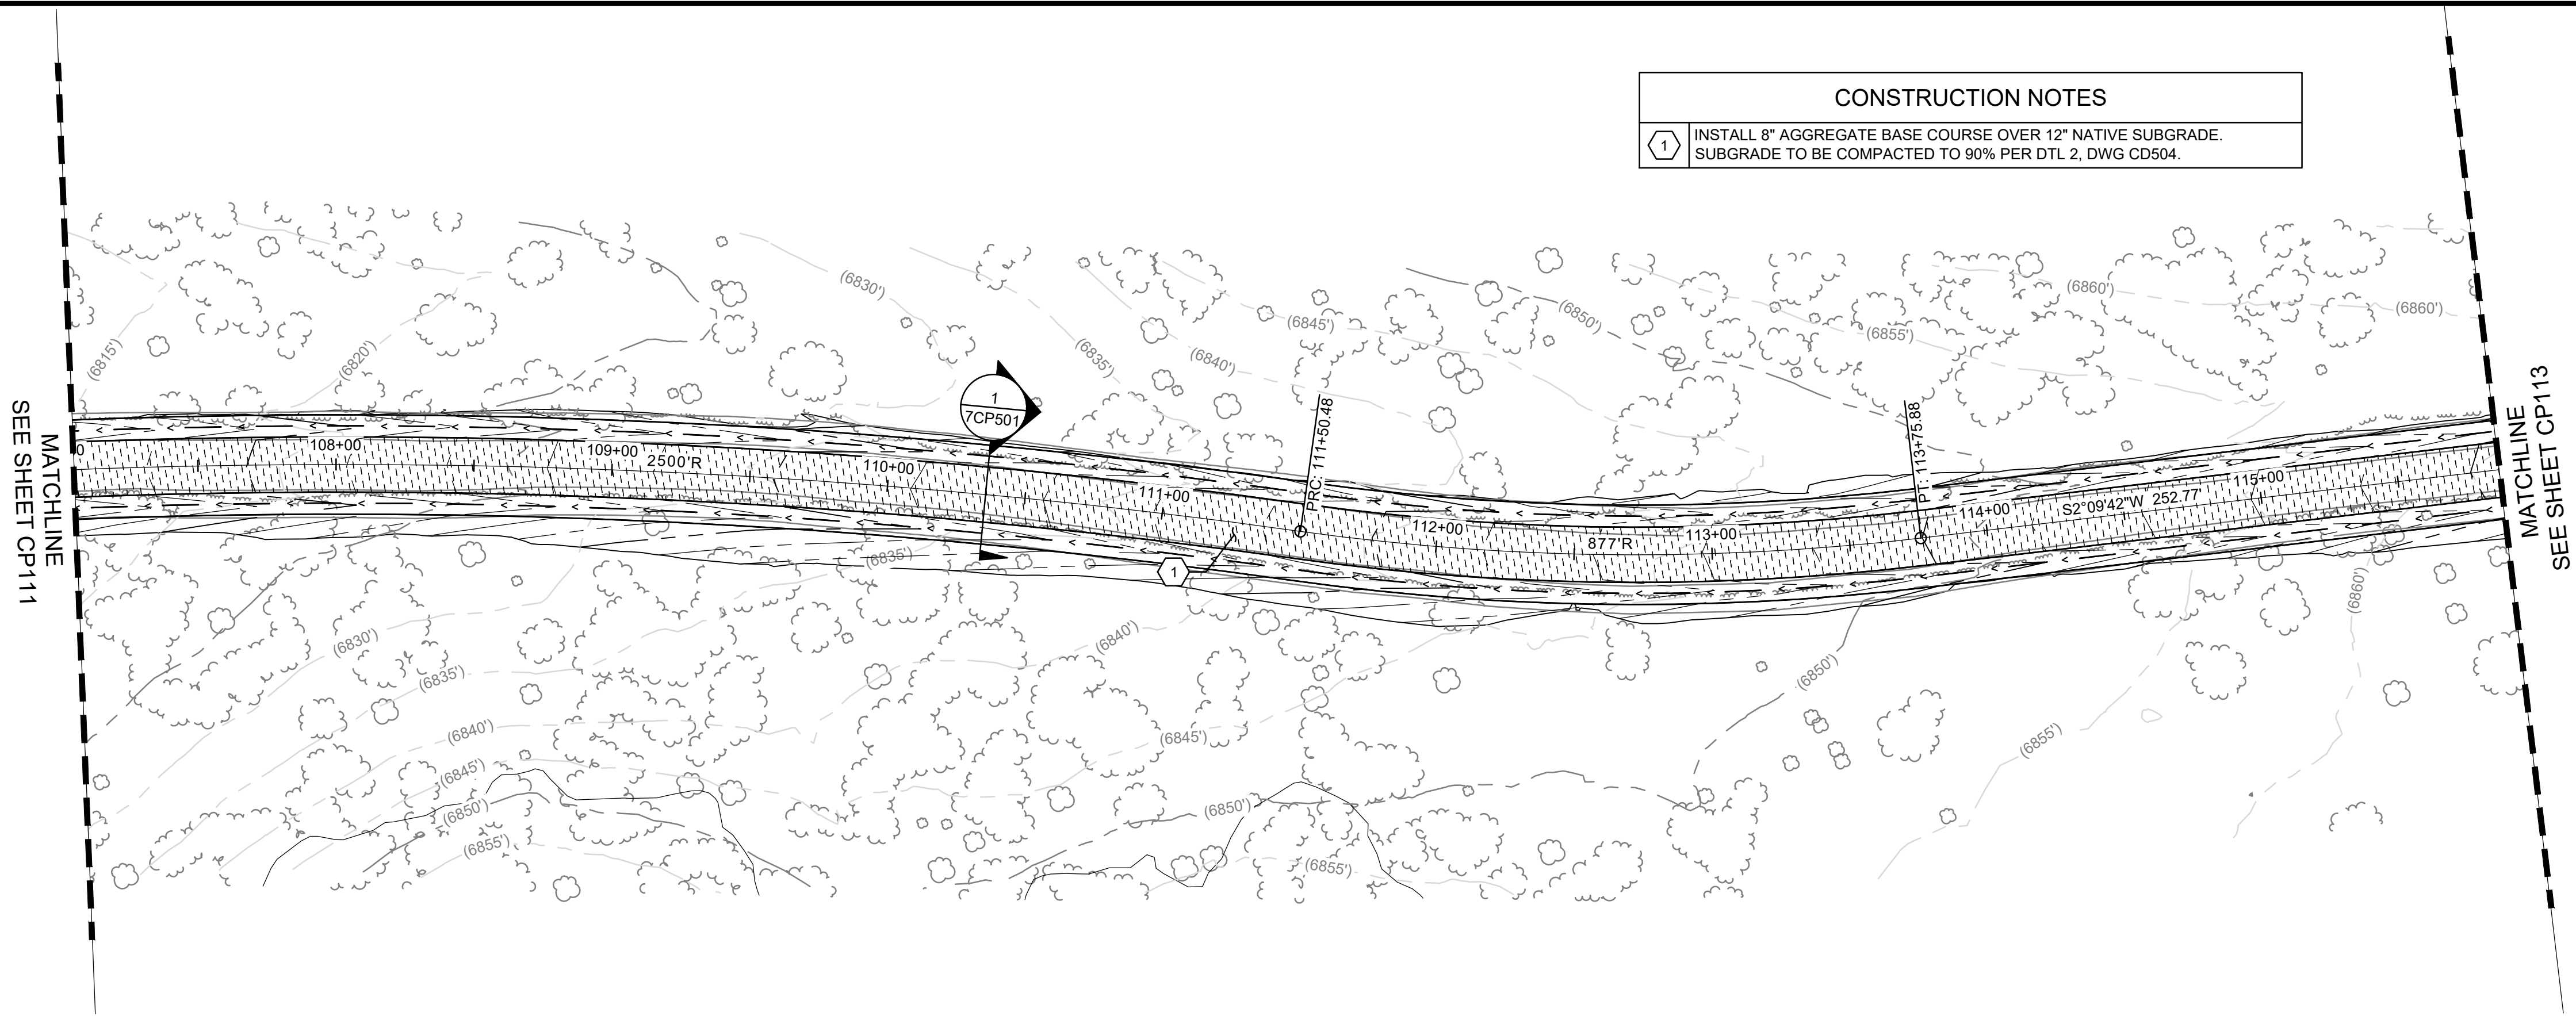

CONSTRUCTION NOTES

1 INSTALL 8" AGGREGATE BASE COURSE OVER 12" NATIVE SUBGRADE.
SUBGRADE TO BE COMPACTED TO 90% PER DTL 2, DWG CD504.

CUT/FILL VOLUMES	
CUT:	1,855 CY
FILL:	4,255 CY
NET:	2,400 CY (FILL)



UNITED STATES DEPARTMENT OF THE INTERIOR
BUREAU OF LAND MANAGEMENT

GARNET HILL RECREATION AREA TITLE I AND II SERVICES

BUREAU OF LAND MANAGEMENT DISTRICT OFFICE
ELY, NEVADA



Project Status	Issue Date
100% CONSTRUCTION DOCUMENTS	12/16/2025
BLM Project #	140L0621D0006
Drawn By	A.BROWN
Checked By	D.KELLEY


07 - POLE LINE ROAD
POLE LINE ROAD PLAN &
PROFILE

7CP112

19 Dec 2025

P:\Projects\BLM - NV & CA\IDOT\Task Orders\Task 27 - Garnet Hill Recreation Area\Task 27 - Garnet Hill Recreation Area Title I & II Services\Engineering\Drawings\Production Drawings\07 - ROAD\208-203-07-CP.dwg 12/16/2025 8:16 AM ABBROWN

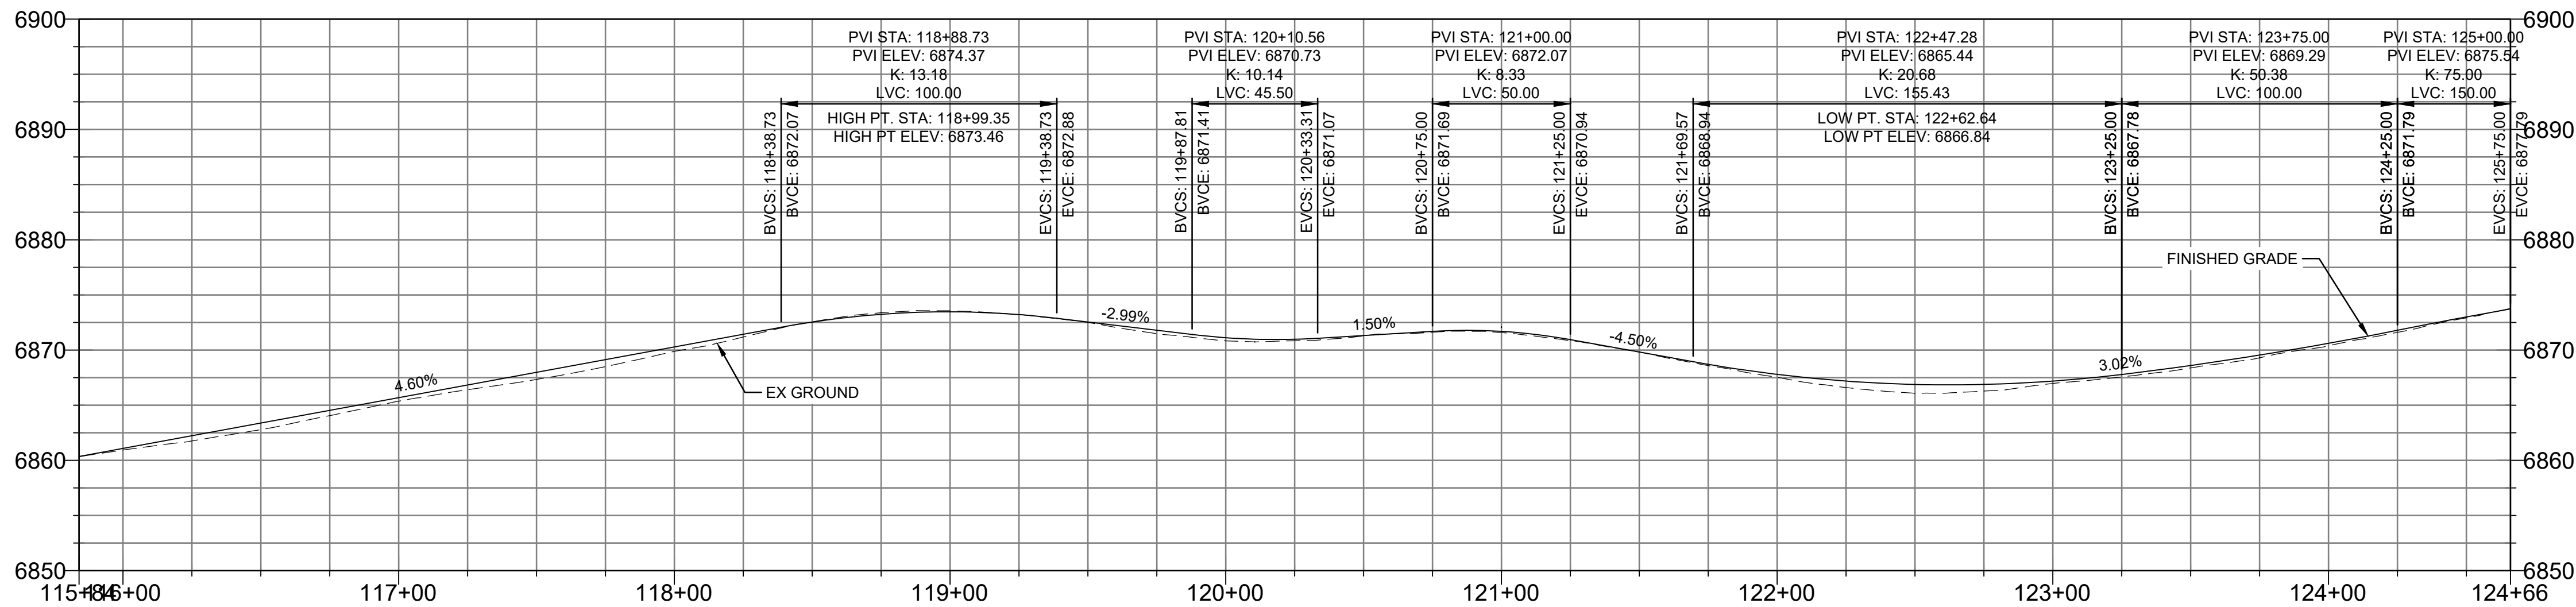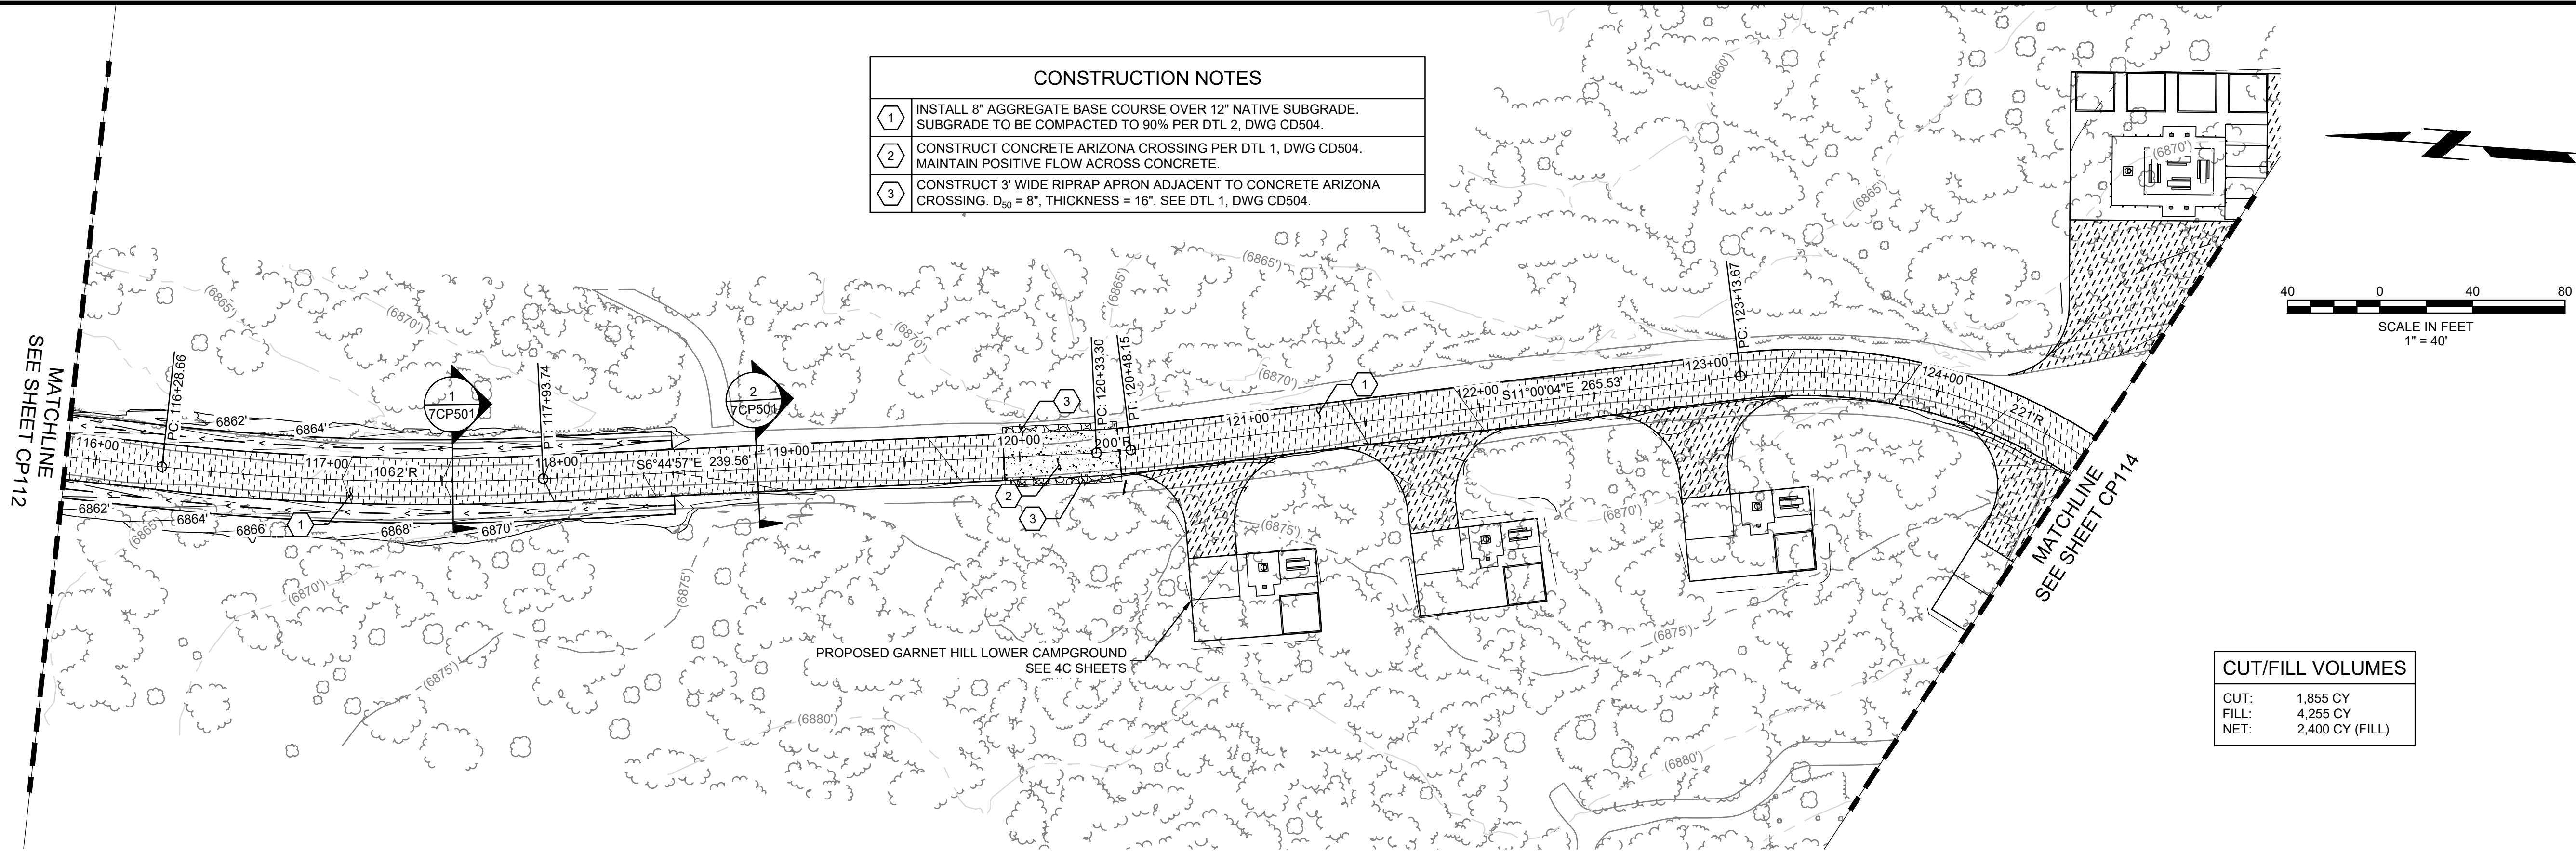

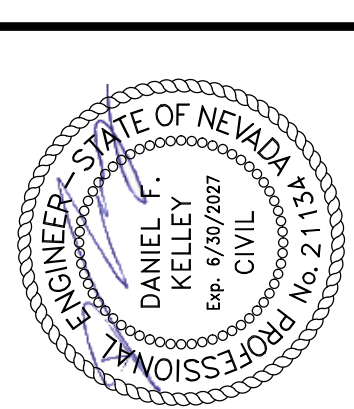

UNITED STATES DEPARTMENT OF THE INTERIOR
BUREAU OF LAND MANAGEMENT

**GARNET HILL RECREATION AREA TITLE I
AND II SERVICES**

BUREAU OF LAND MANAGEMENT DISTRICT OFFICE
ELY, NEVADA



Project Status
100% CONSTRUCTION DOCUMENTS
BLM Project # 140L0621D0006
Drawn By ABBROWN
Checked By D.KELLEY

Issue Date
12/16/2025

07 - POLE LINE ROAD
POLE LINE ROAD PLAN &
PROFILE

7CP113

P:\Projects\BLM - NV & CA\IDOT\Task Orders\Task 27 - Garnet Hill Recreation Area\Task 27 - Garnet Hill Recreation Area\Drawings\07 - Road\208-203-07-CP.dwg 12/16/2025 8:16 AM ABBROWN

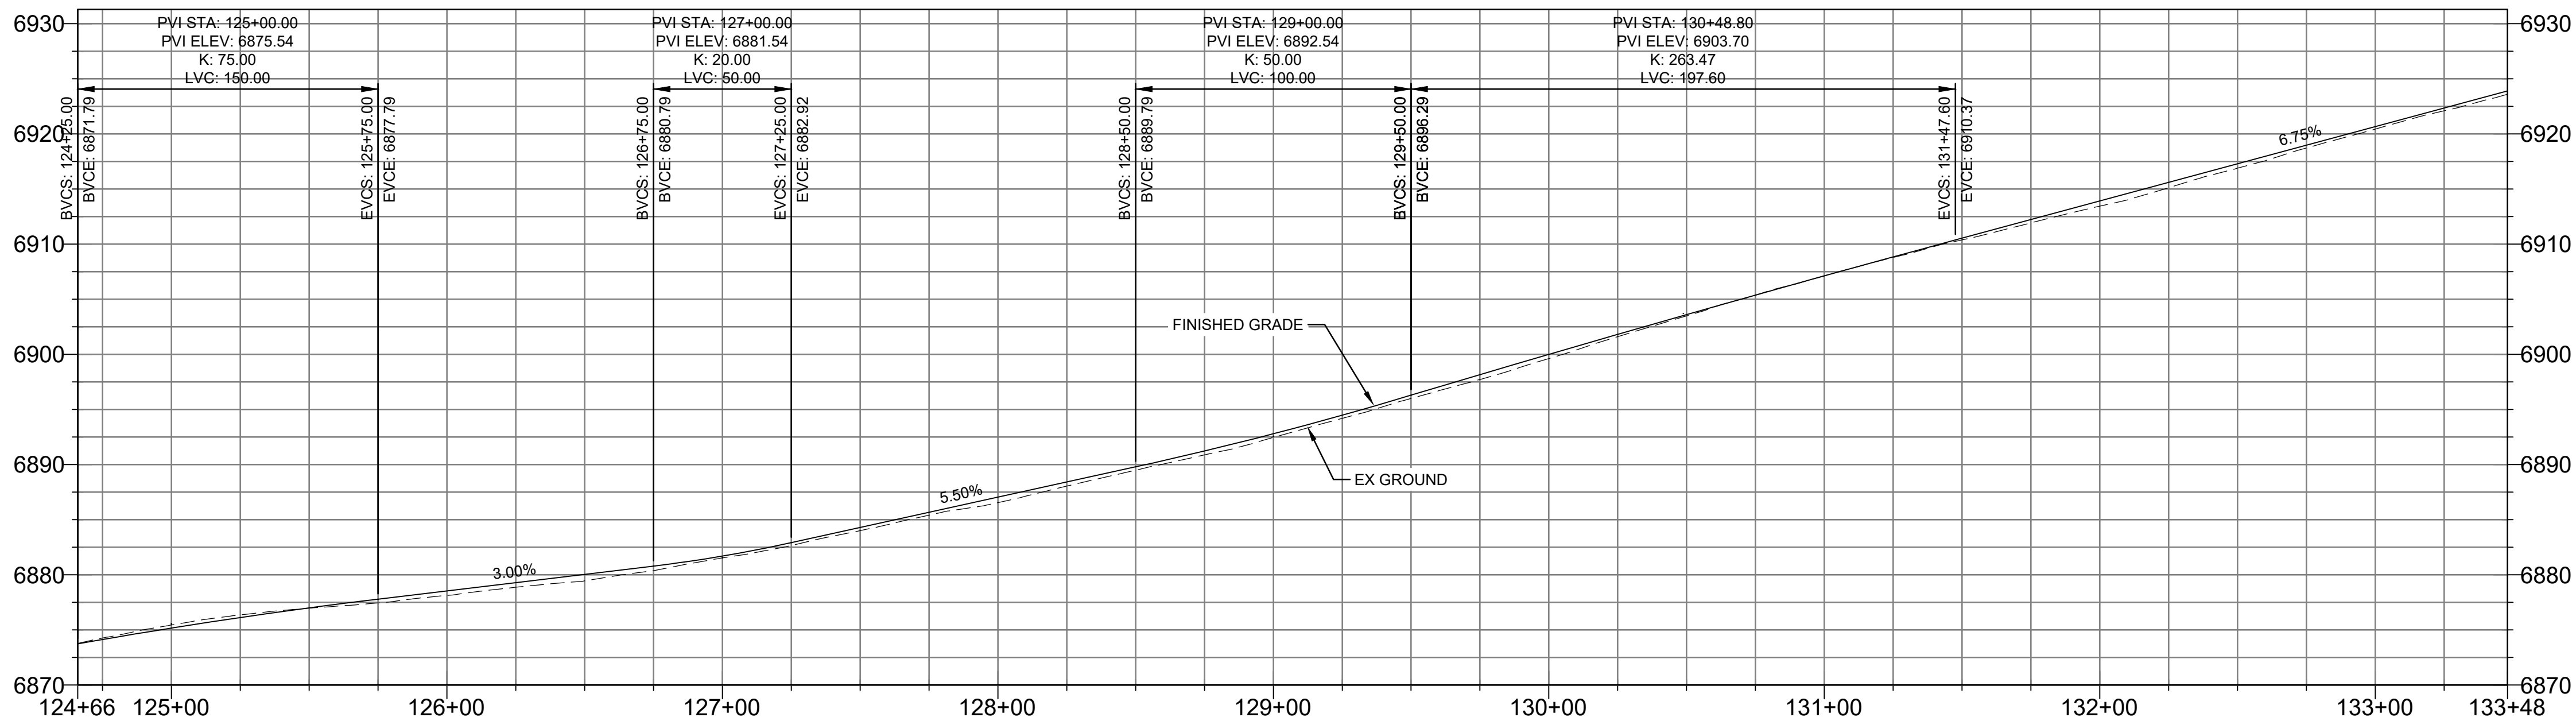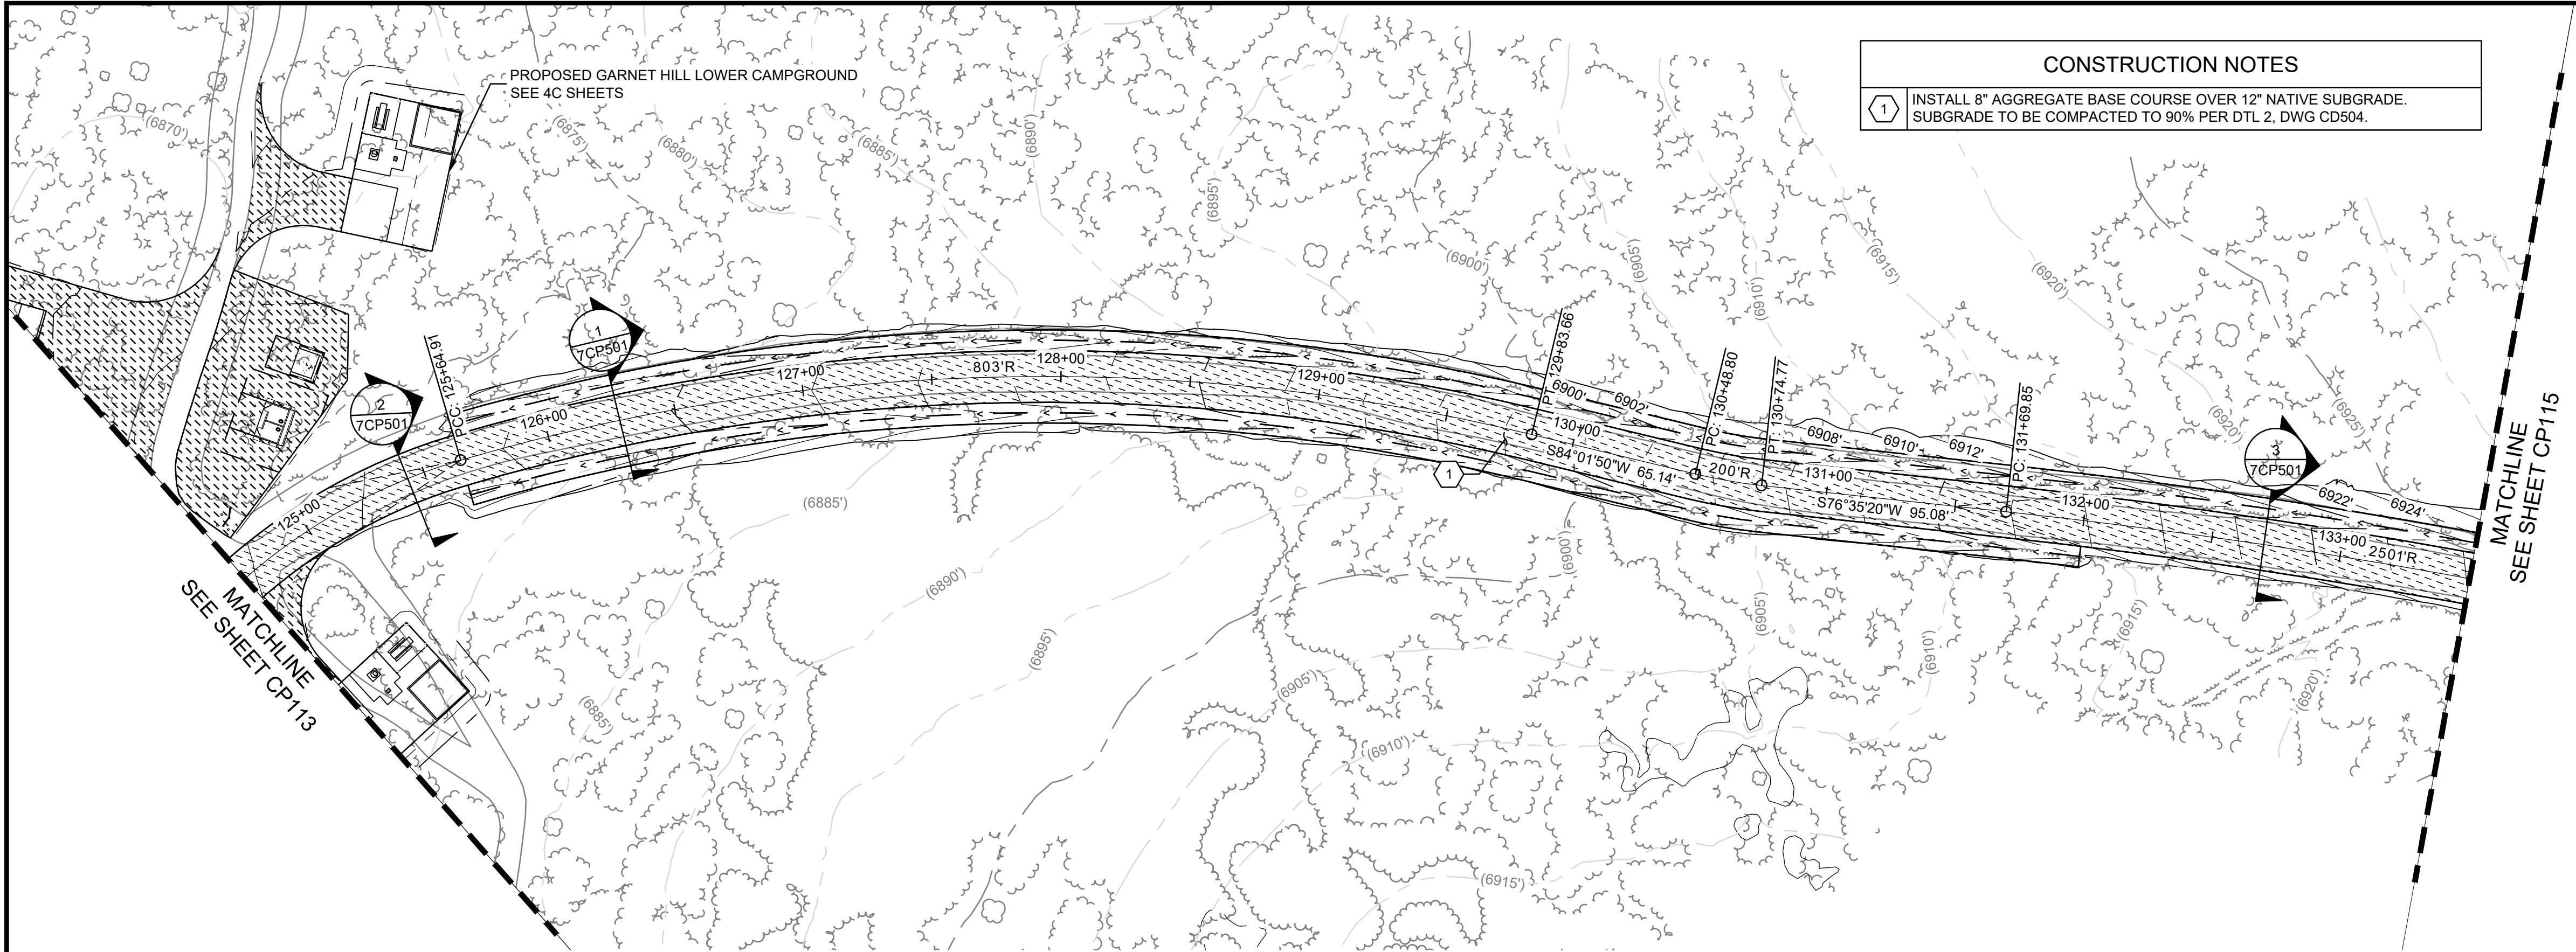

NATIONAL SYSTEM OF PUBLIC LANDS
U.S. DEPARTMENT OF THE INTERIOR
BUREAU OF LAND MANAGEMENT

U.S. DEPARTMENT OF THE INTERIOR
BUREAU OF LAND MANAGEMENT
MARCH 3, 1881

ENGINEER
STATE OF NEVADA
DANIEL F. KELLEY
No. 21134
19 Dec 2025

UNITED STATES DEPARTMENT OF THE INTERIOR
BUREAU OF LAND MANAGEMENT

**GARNET HILL RECREATION AREA TITLE I
AND II SERVICES**

BUREAU OF LAND MANAGEMENT DISTRICT OFFICE
ELY, NEVADA

Issue Date
12/16/2025

Project Status
100% CONSTRUCTION DOCUMENTS

BLM Project #
140L0621D0006

Drawn By
ABBROWN

Checked By
D.KELLEY



Revision Issue
Description

Rev. #

07 - POLE LINE ROAD
POLE LINE ROAD PLAN &
PROFILE

7CP114

P:\Projects\BLM - NV & CA\IDOT\Task Orders\Task 27 - Garnet Hill Recreation Area Title I & II Services\Engineering\Drawings\Production Drawings\07 - ROAD\208-203-07-CP.dwg 12/16/2025 8:16 AM ABBROWN

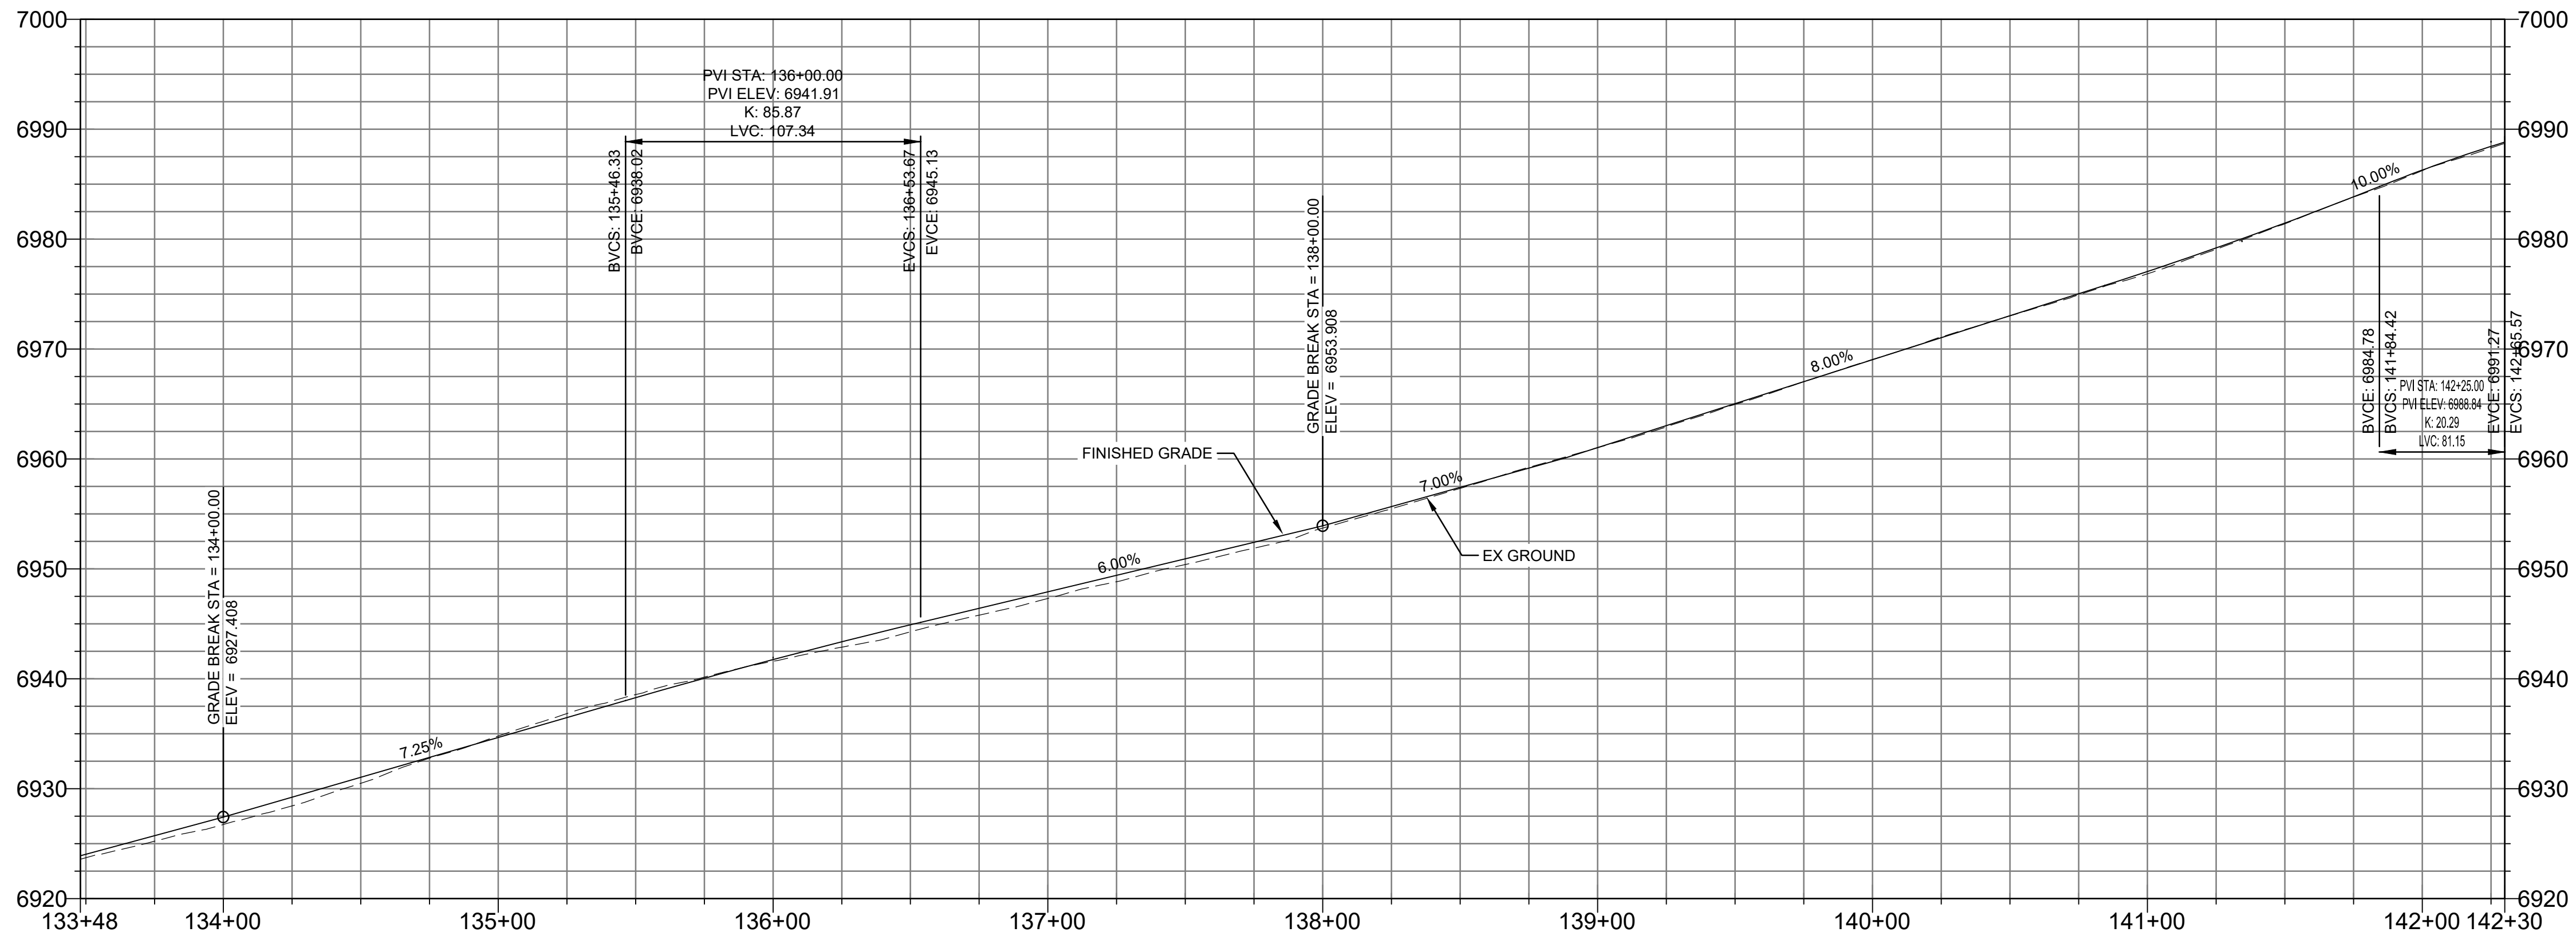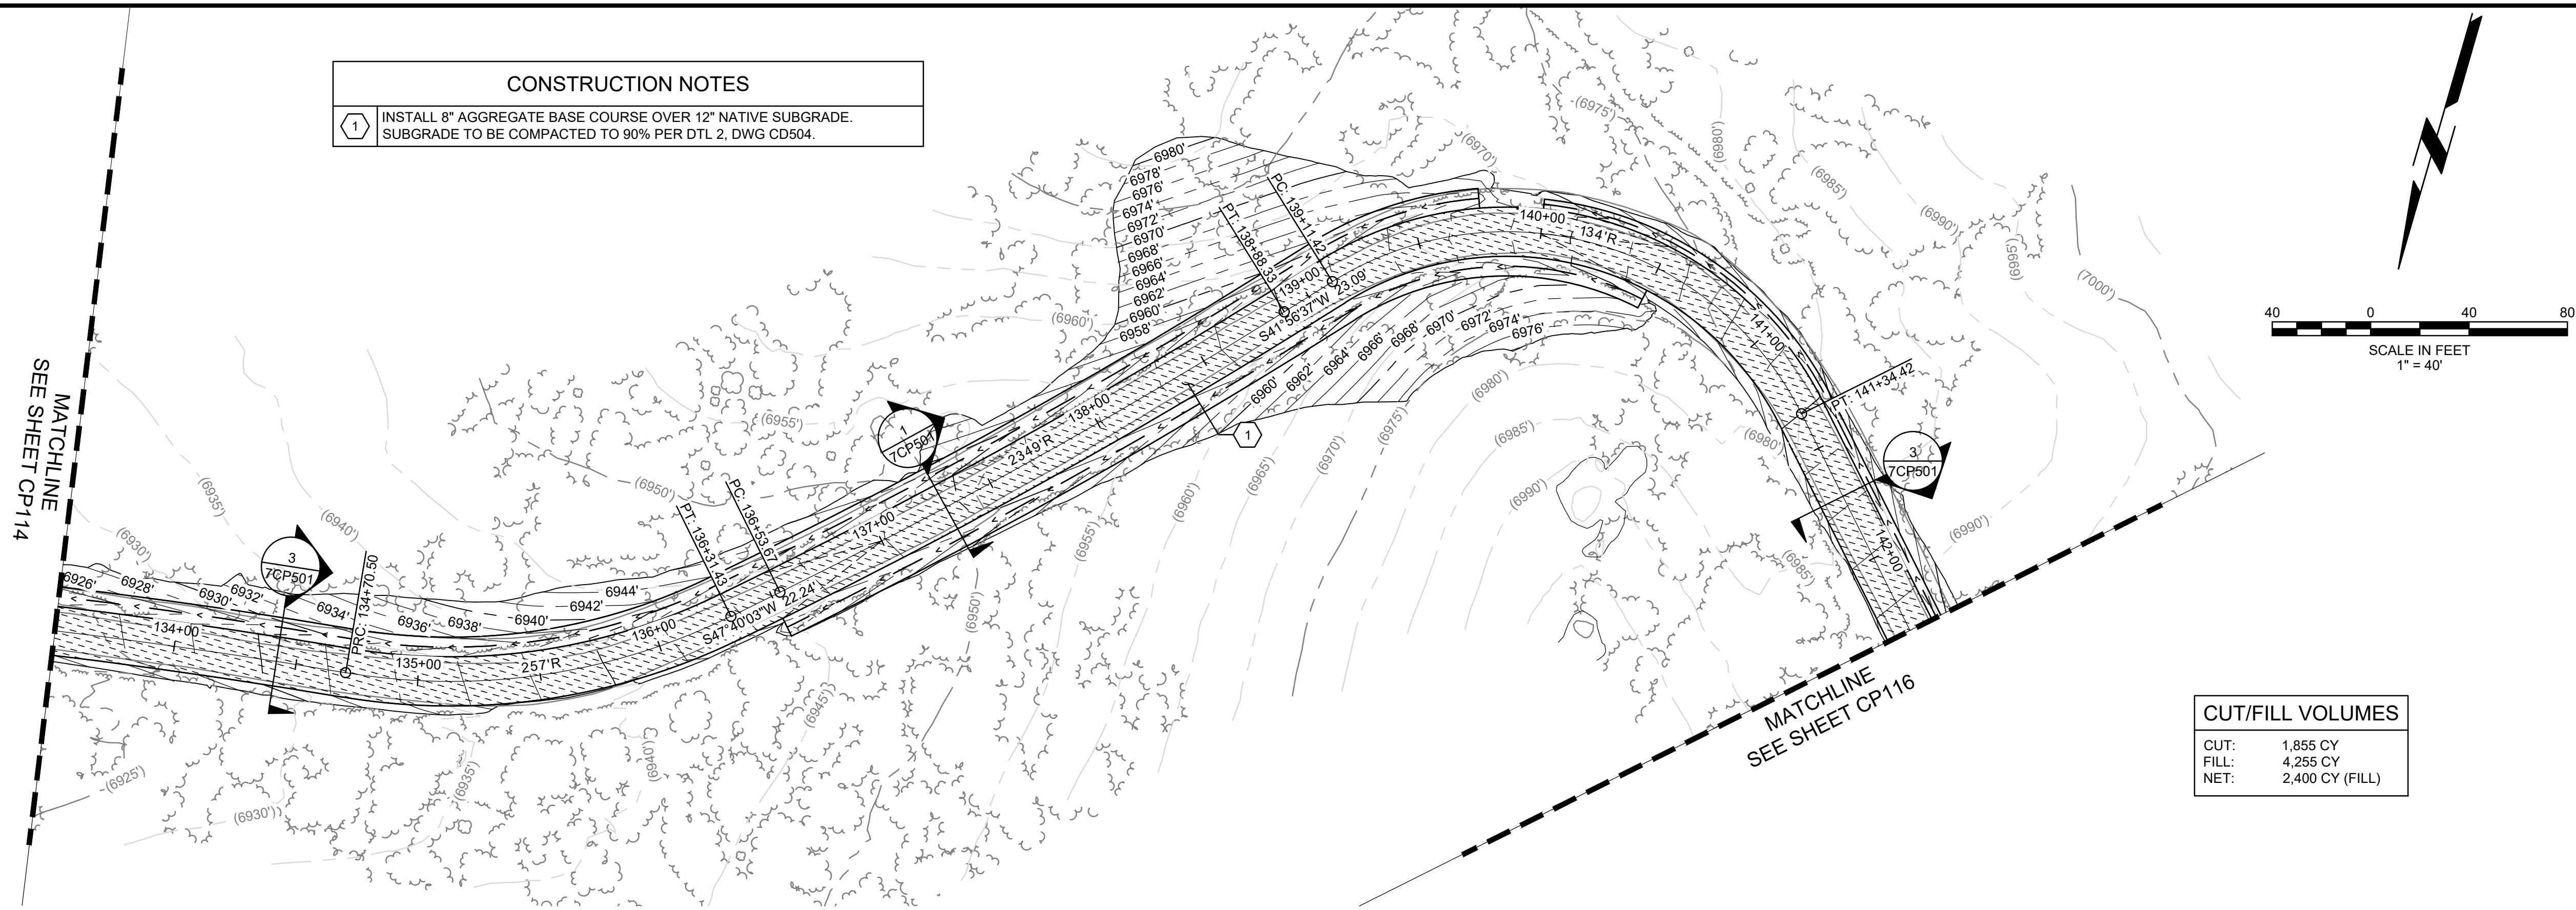

NATIONAL SYSTEM OF PUBLIC LANDS
U.S. DEPARTMENT OF THE INTERIOR
BUREAU OF LAND MANAGEMENT

U.S. DEPARTMENT OF THE INTERIOR
BUREAU OF LAND MANAGEMENT
MARCH 3, 1891

STATE OF NEVADA
DANIEL F. KELLEY
No. 21134
Professional Engineer
19 Dec 2025

UNITED STATES DEPARTMENT OF THE INTERIOR
BUREAU OF LAND MANAGEMENT

**GARNET HILL RECREATION AREA TITLE I
AND II SERVICES**

BUREAU OF LAND MANAGEMENT DISTRICT OFFICE
ELY, NEVADA

Issue Date
12/16/2025

Project Status
100% CONSTRUCTION DOCUMENTS

BLM Project #
140L0621D0006

Drawn By
A. BROWN

Checked By
D. KELLEY



Revision Issue
Description


Rev. #

07 - POLE LINE ROAD
POLE LINE ROAD PLAN &
PROFILE

7CP115

P:\Projects\BLM - NV & CA ID\Task Orders\Task 27 - Garnet Hill Recreation Area\Task 27 - Garnet Hill Recreation Area\Drawings\07 - ROAD\208-203-07-CP.dwg 12/16/2025 8:16 AM A.BROWN

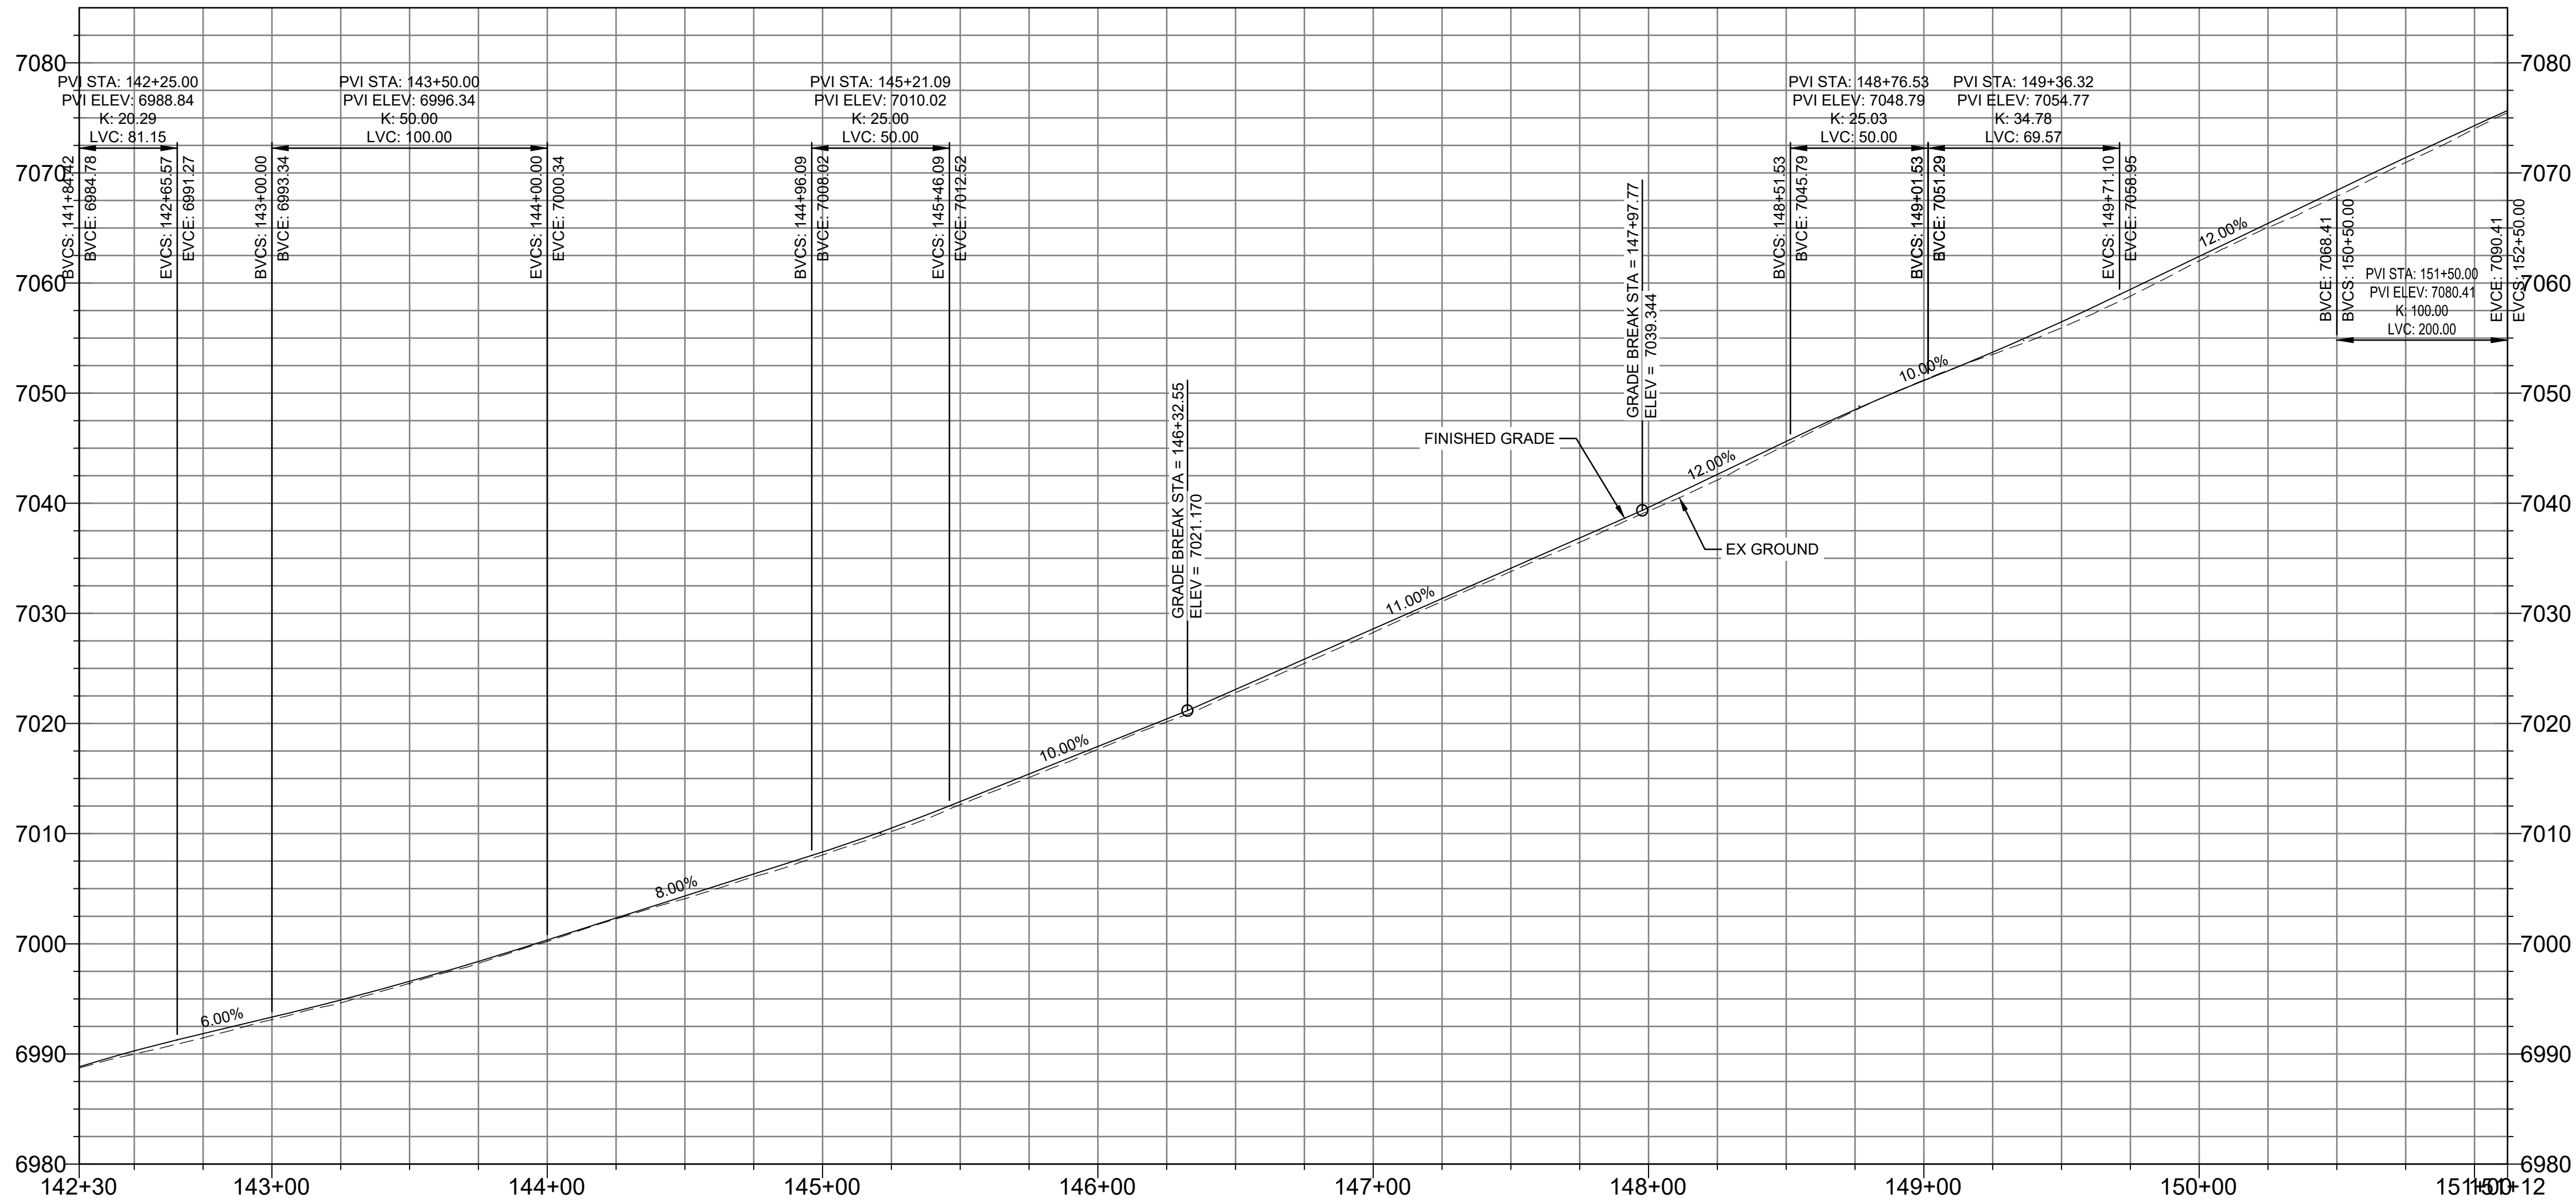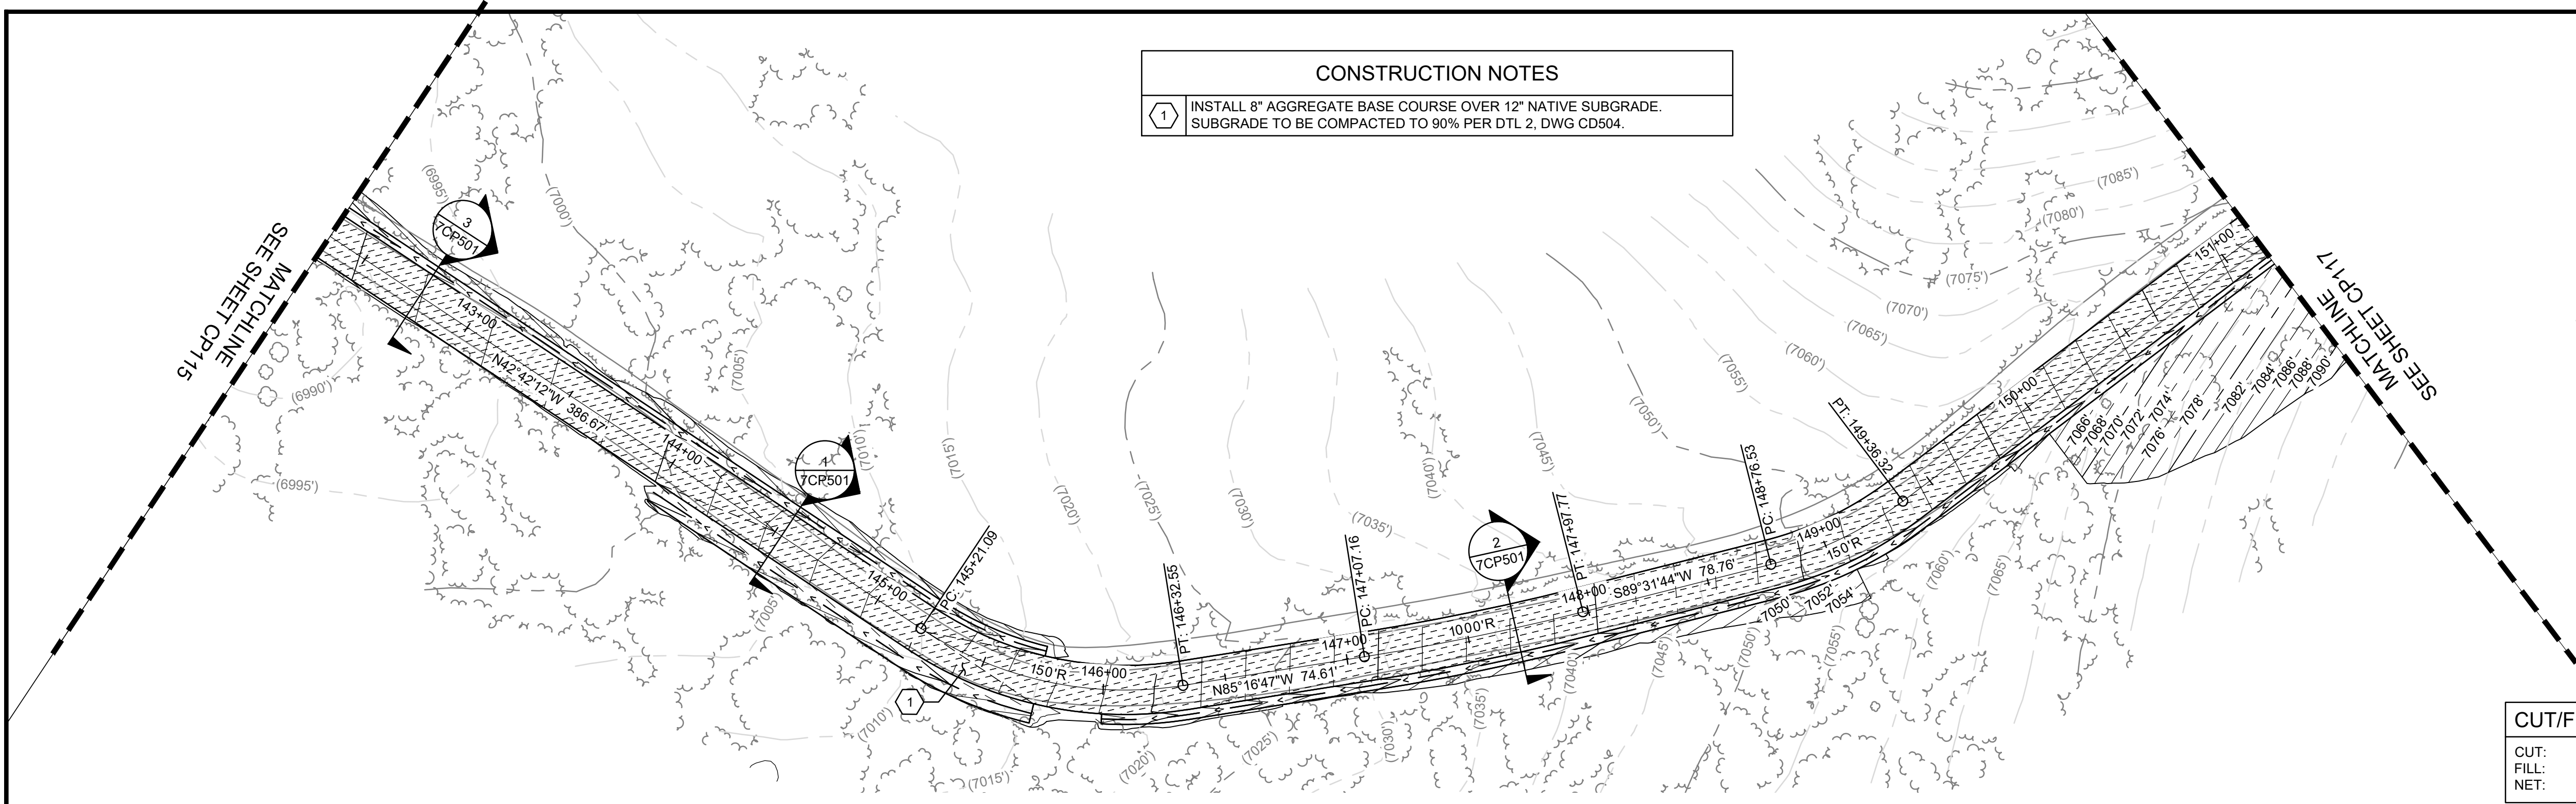

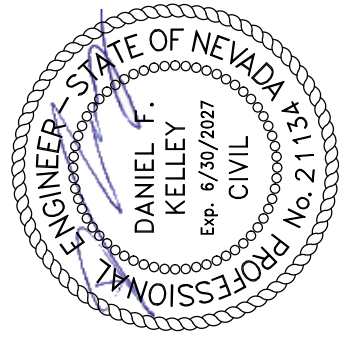

UNITED STATES DEPARTMENT OF THE INTERIOR
BUREAU OF LAND MANAGEMENT

**GARNET HILL RECREATION AREA TITLE I
AND II SERVICES**

BUREAU OF LAND MANAGEMENT DISTRICT OFFICE
ELY, NEVADA

Issue Date
12/16/2025

Project Status
100% CONSTRUCTION DOCUMENTS

BLM Project #
140L0621D0006

Drawn By
A.BROWN



Checked By
D.KELLEY


07 - POLE LINE ROAD
POLE LINE ROAD PLAN &
PROFILE

7CP116

19 Dec 2025

P:\Projects\BLM - NV & CA\IDOT\Task Orders\Task 27 - Garnet Hill Recreation Area\Task 27 - Garnet Hill Recreation Area\Drawings\07 - ROAD\208-203-07-CP.dwg 12/16/2025 8:16 AM ABBROWN

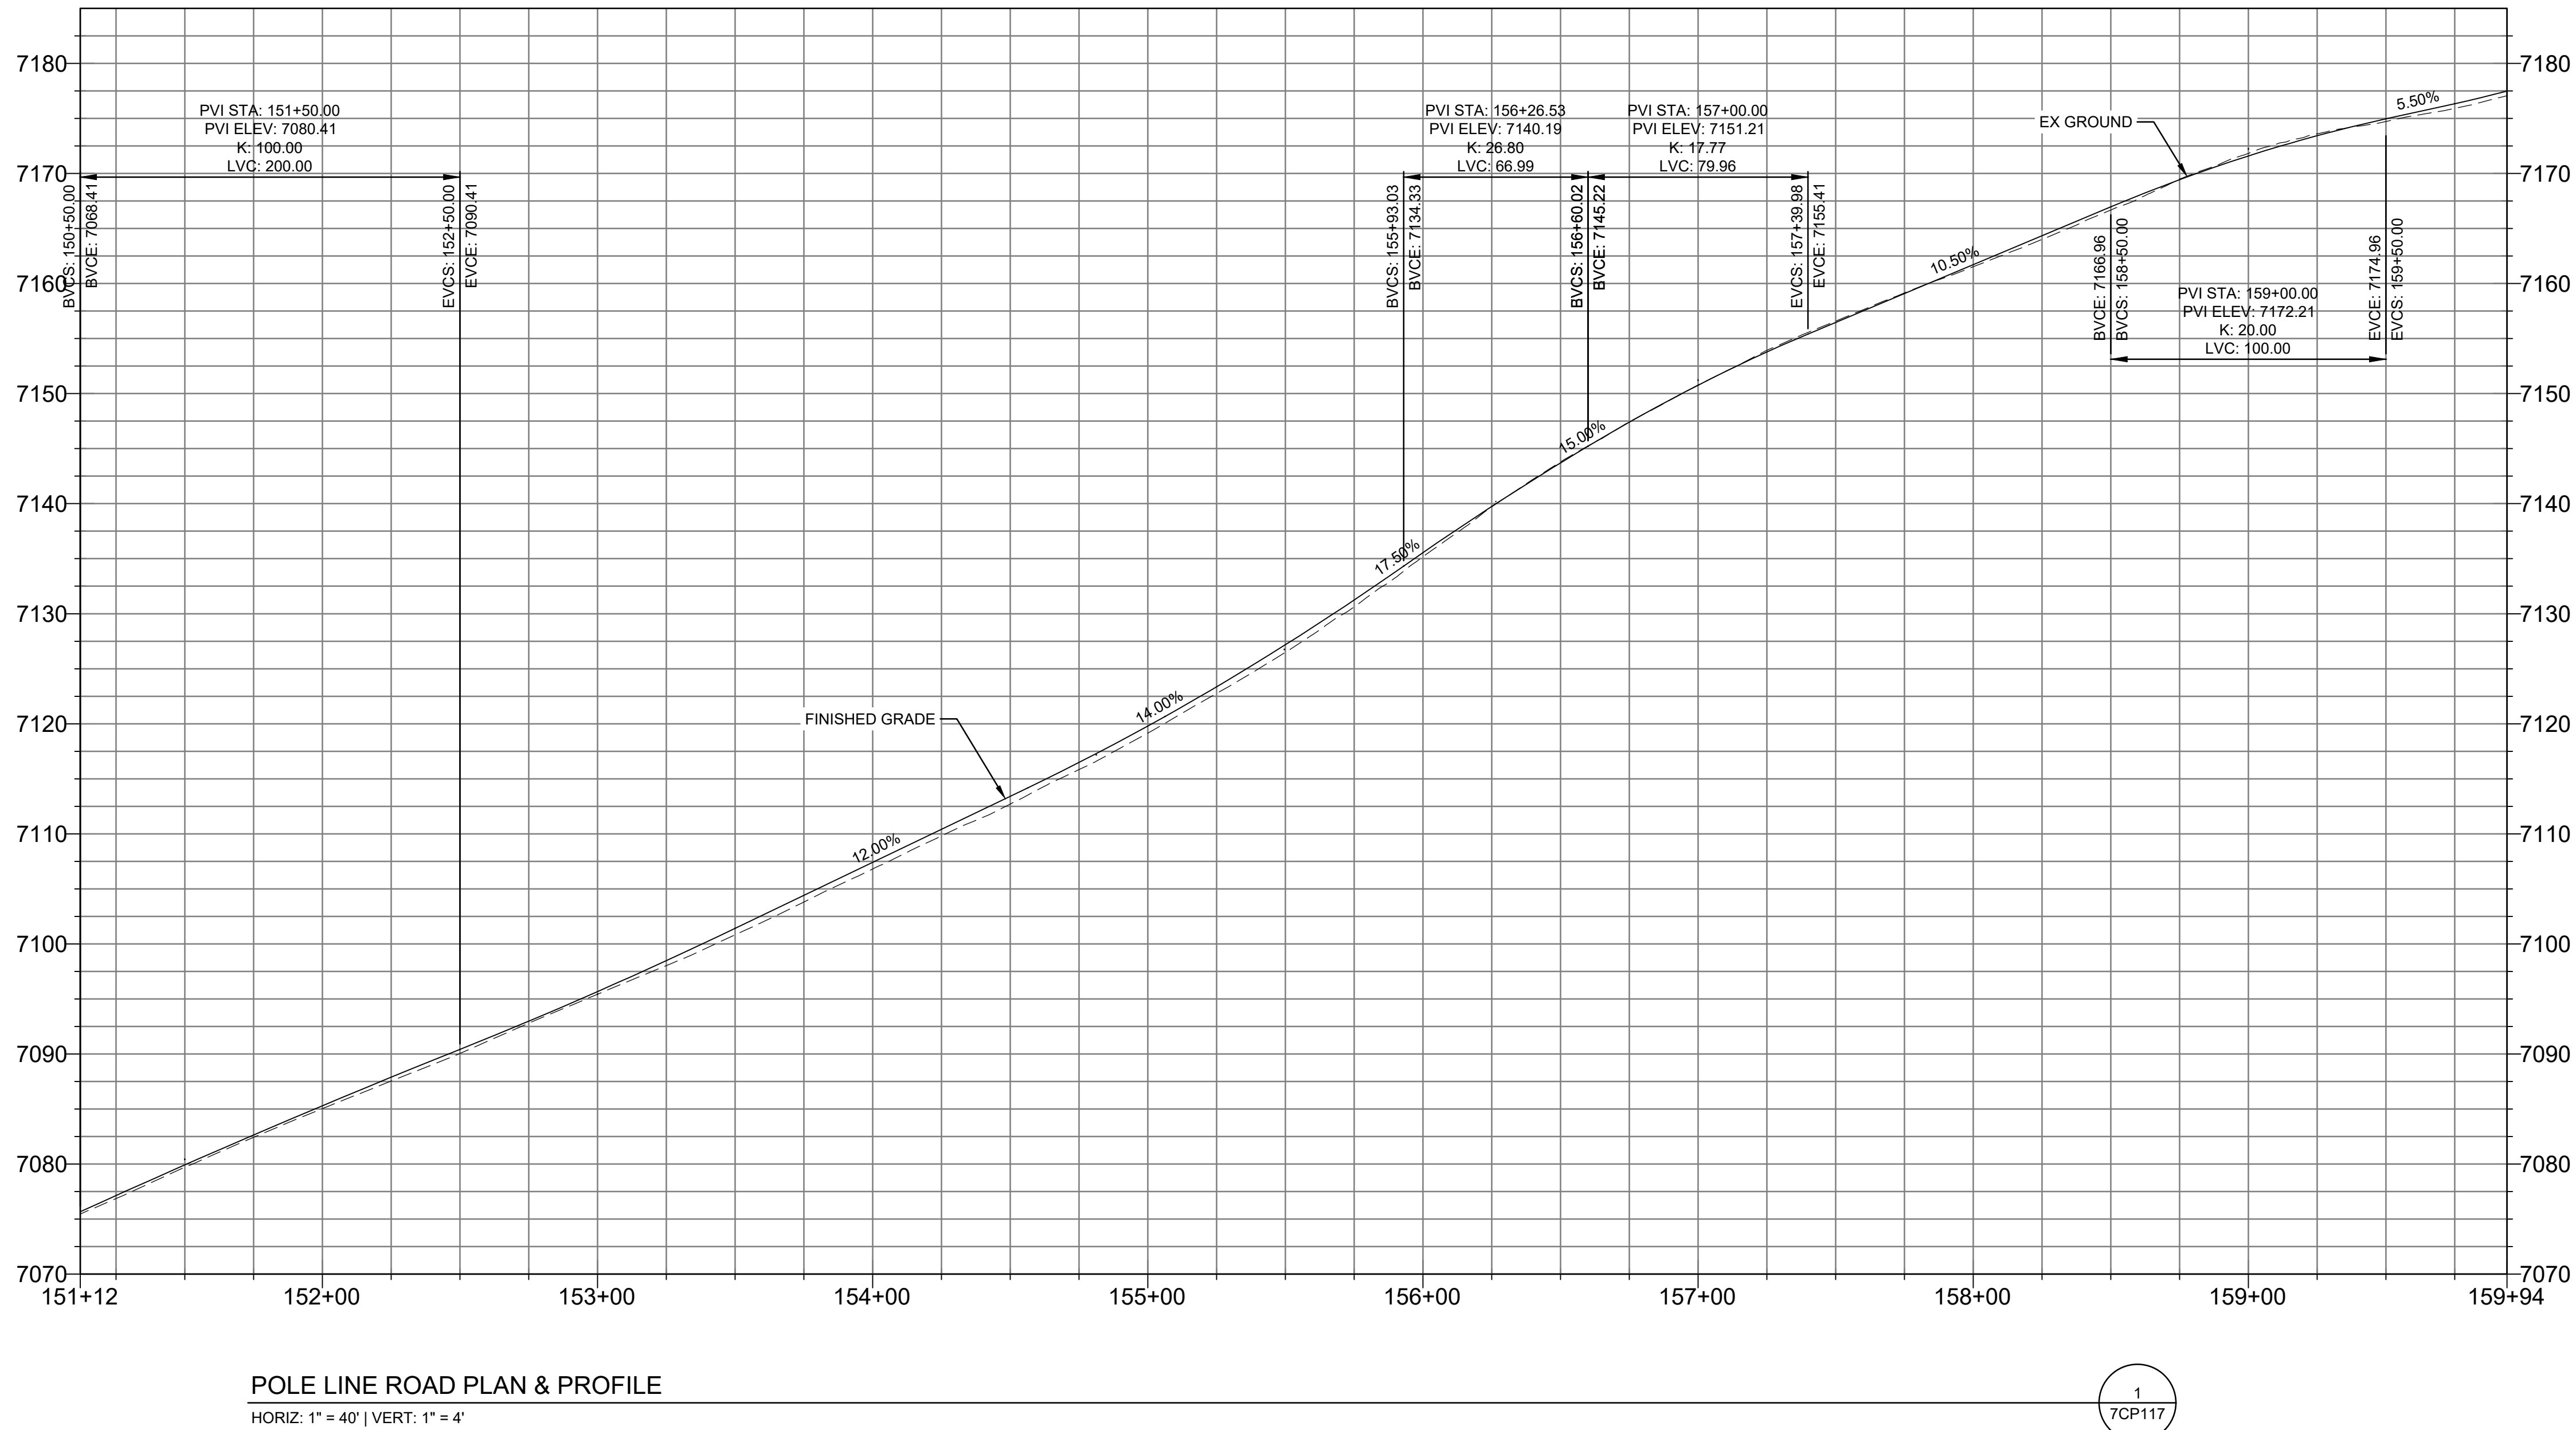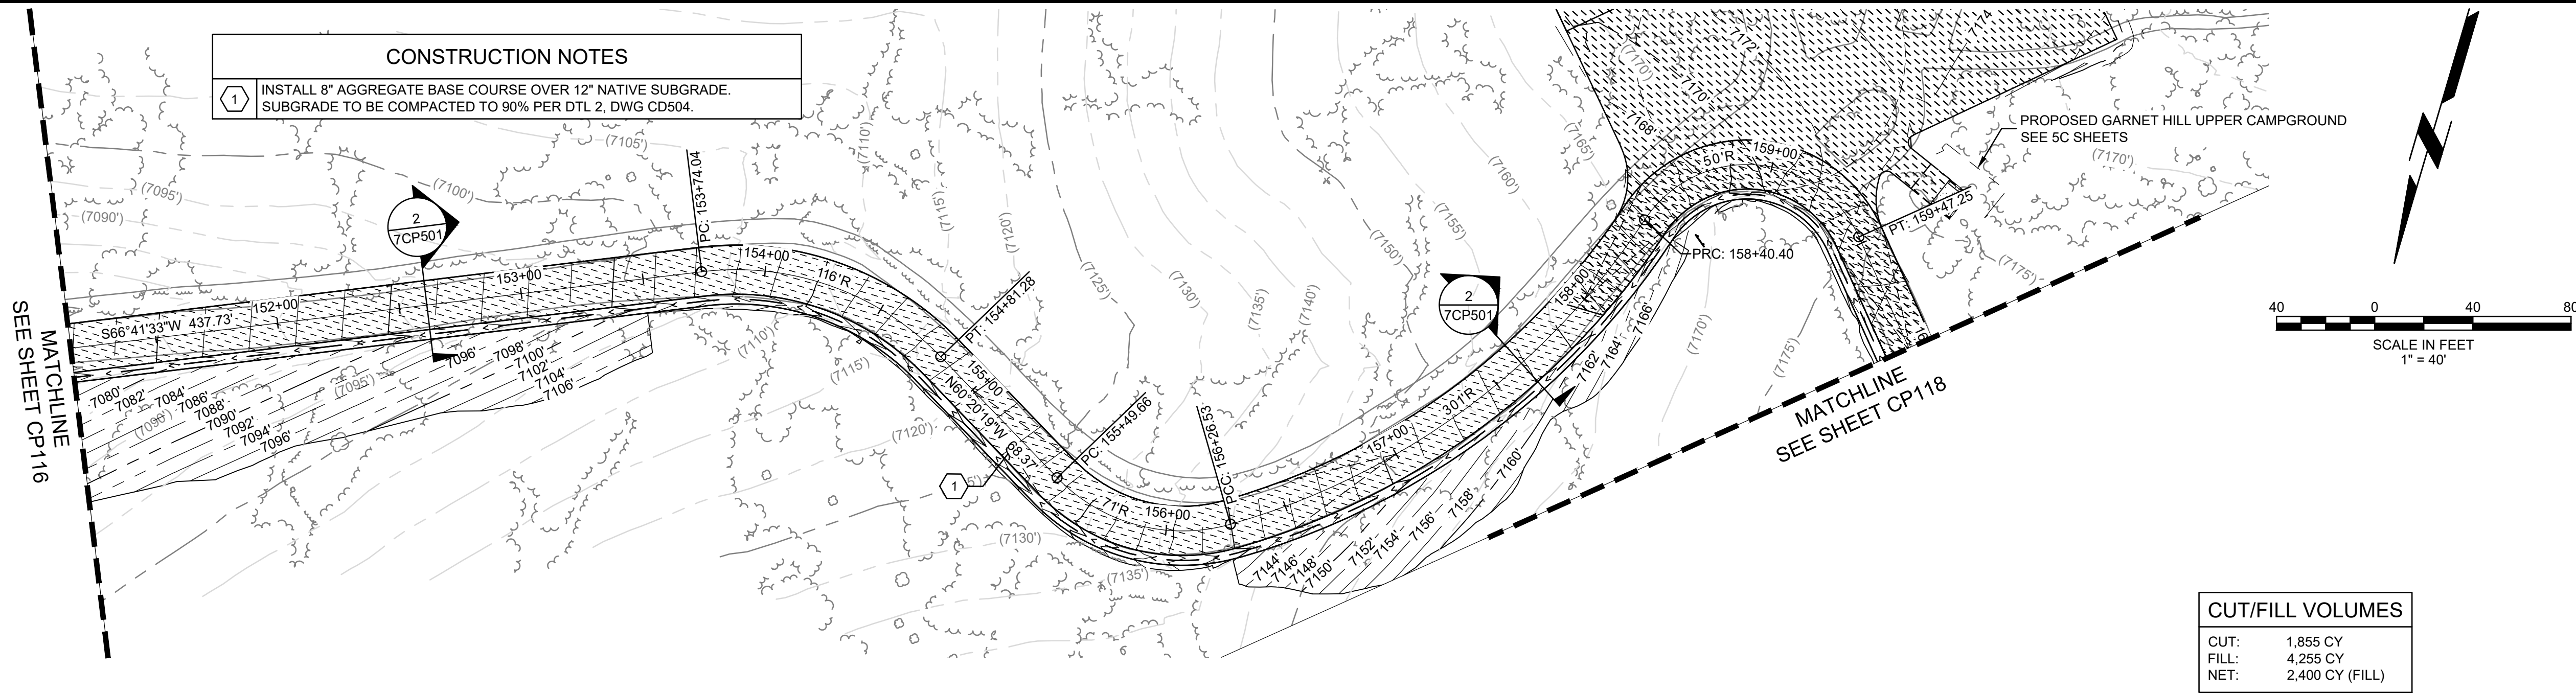

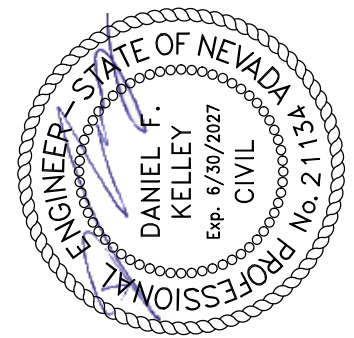

UNITED STATES DEPARTMENT OF THE INTERIOR
BUREAU OF LAND MANAGEMENT

**GARNET HILL RECREATION AREA TITLE I
AND II SERVICES**

BUREAU OF LAND MANAGEMENT DISTRICT OFFICE
ELY, NEVADA

Project Status
100% CONSTRUCTION DOCUMENTS
BLM Project # 140L0621D0006
Drawn By ABBROWN
Checked By D.KELLEY

Issue Date
12/16/2025



Revision Issue

Rev. #	Description	Date
--------	-------------	------


07 - POLE LINE ROAD
POLE LINE ROAD PLAN &
PROFILE

7CP117

19 Dec 2025

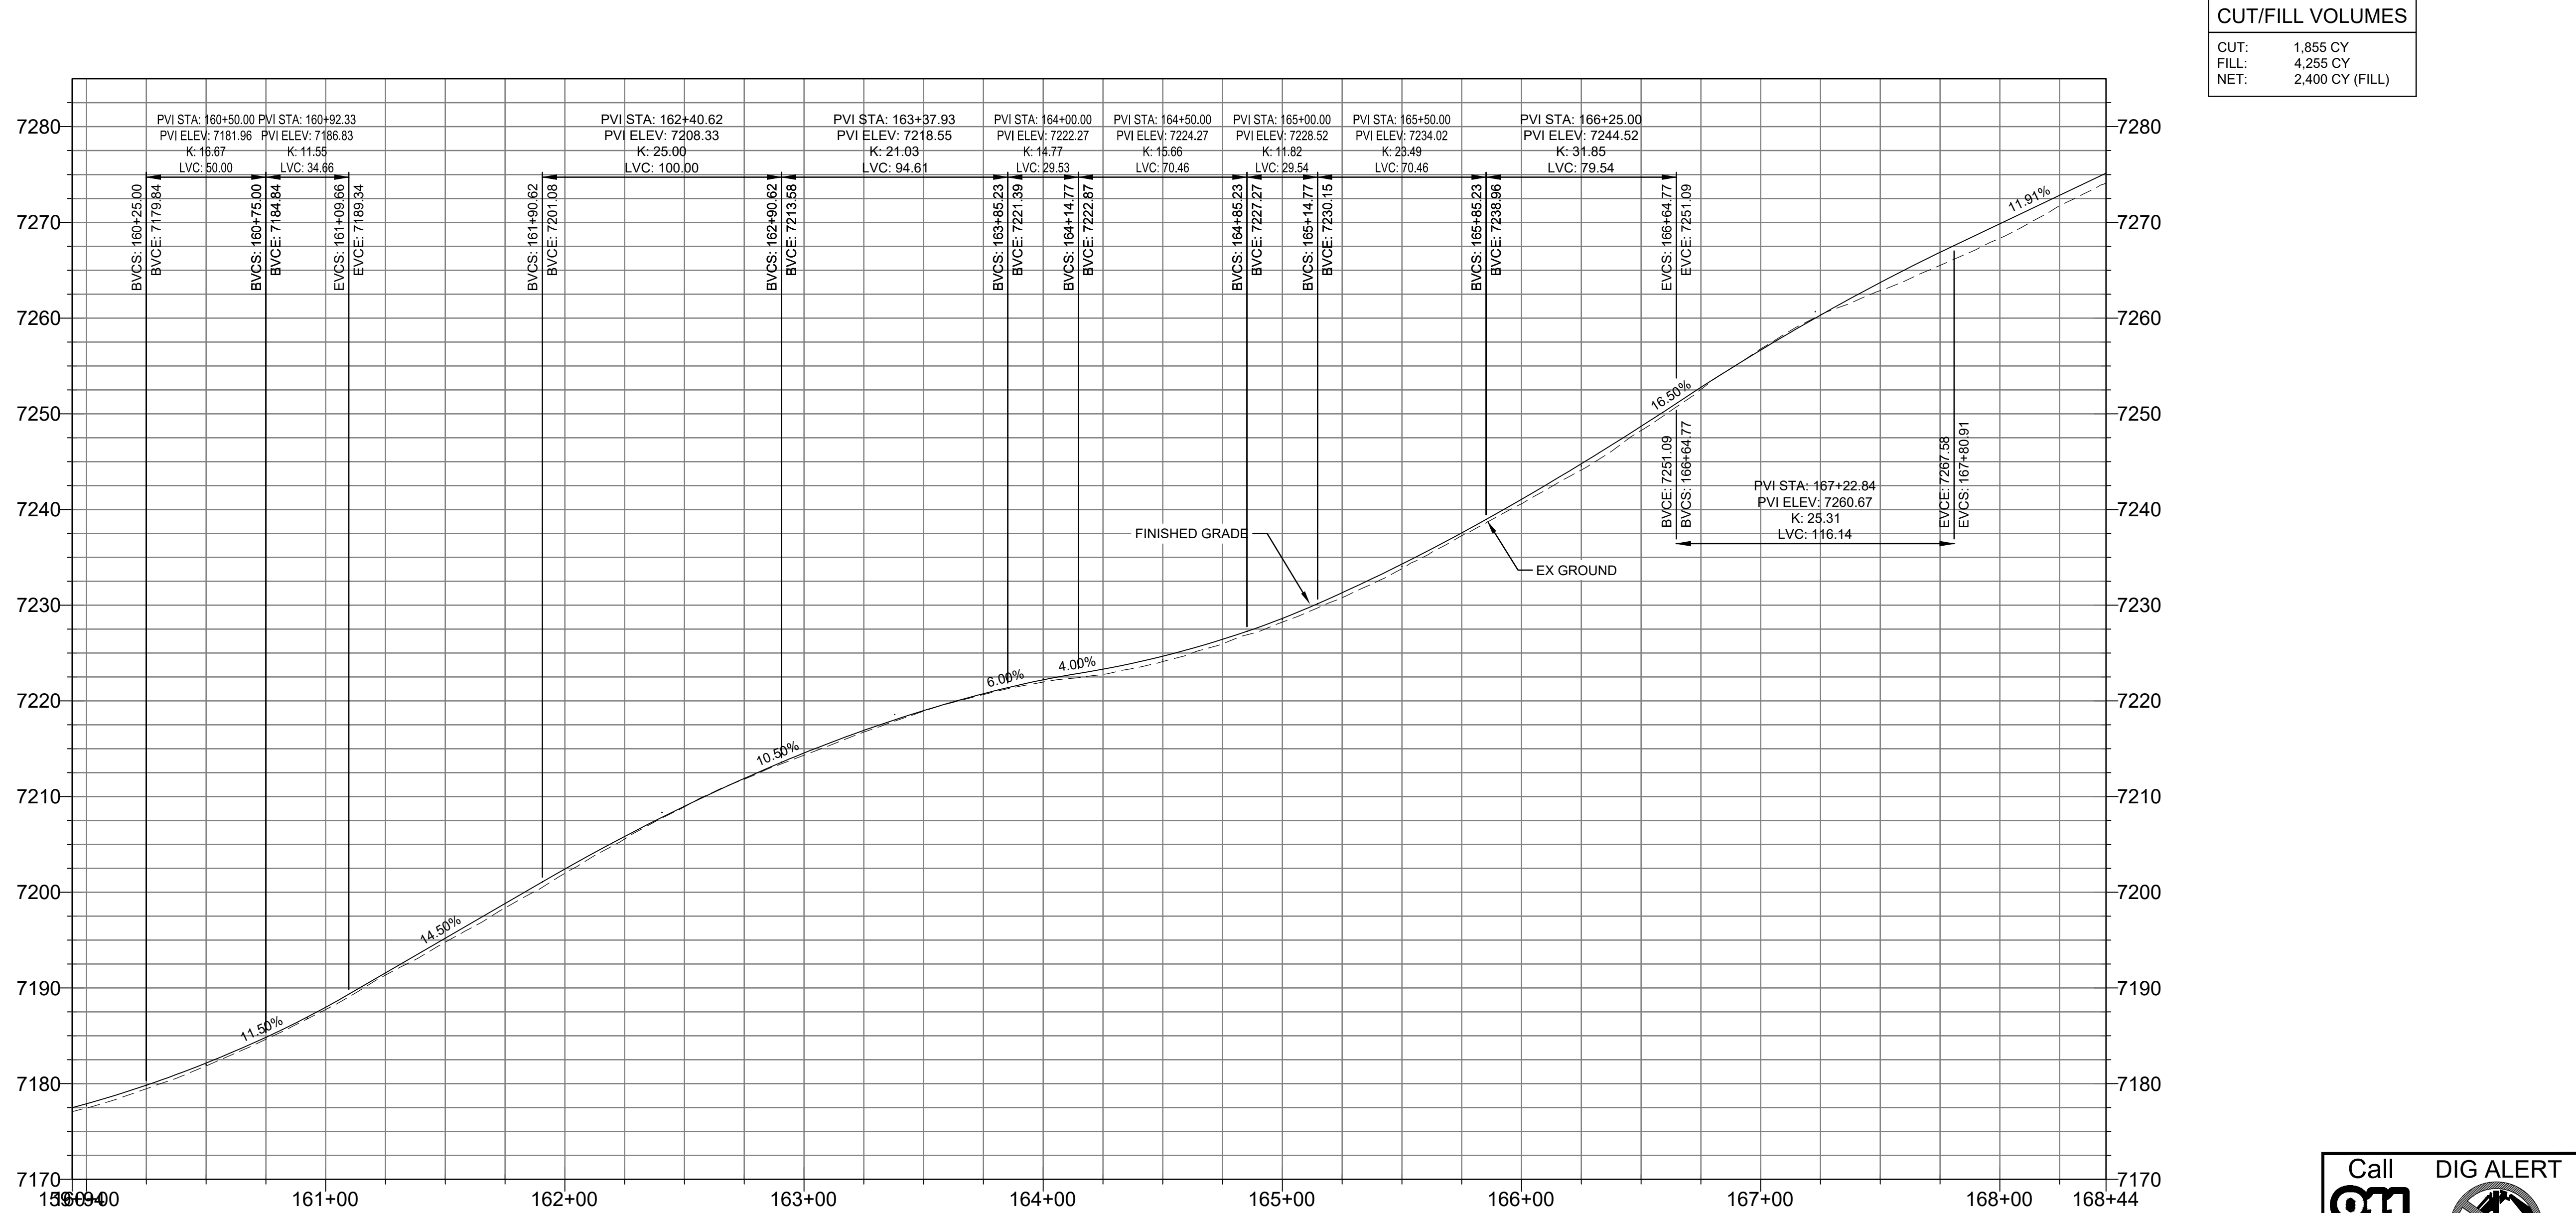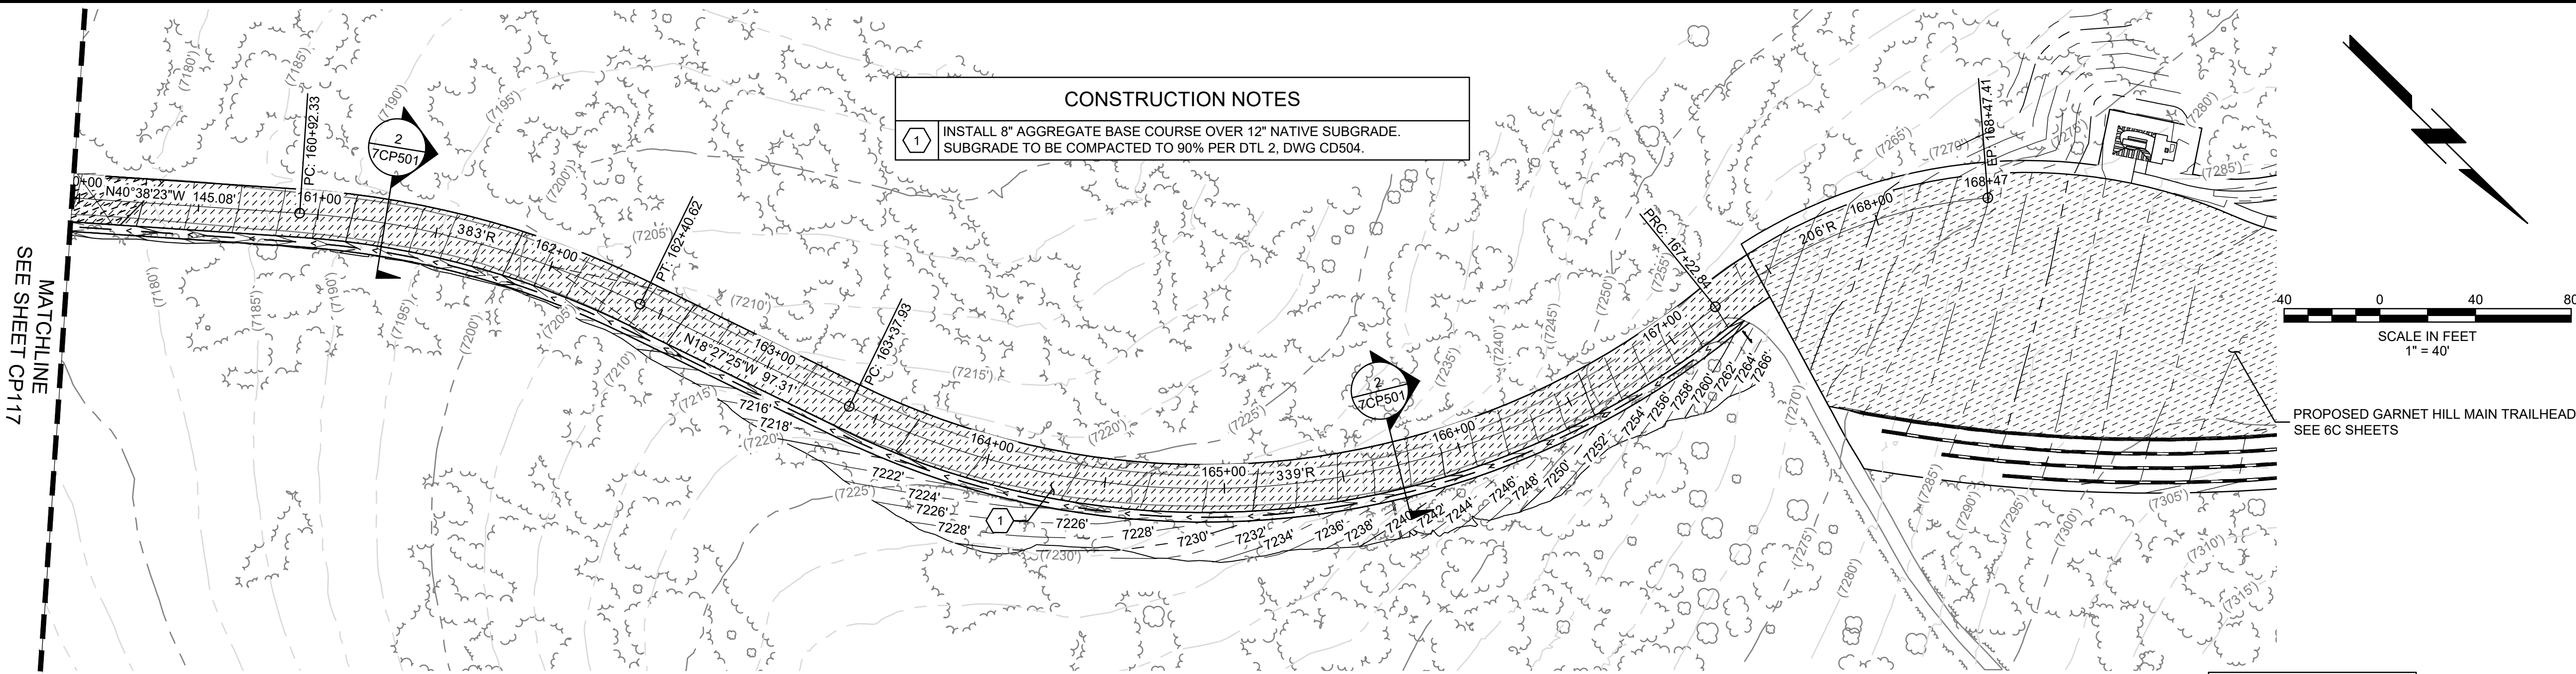

P:\Projects\BLM - NV & CA\IDOT\Task Orders\Task 27 - Garnet Hill Recreation Area\Task 27 - Garnet Hill Recreation Area\Drawings\07 - ROAD\208-203-07-CP.dwg 12/16/2025 8:16 AM ABBROWN

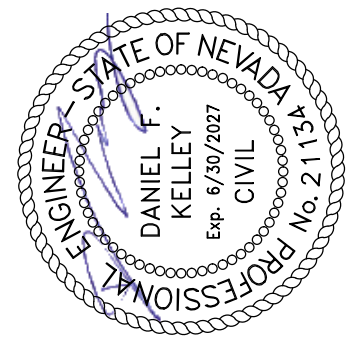

UNITED STATES DEPARTMENT OF THE INTERIOR
BUREAU OF LAND MANAGEMENT

**GARNET HILL RECREATION AREA TITLE I
AND II SERVICES**

BUREAU OF LAND MANAGEMENT DISTRICT OFFICE
ELY, NEVADA

Issue Date
12/16/2025

Project Status
100% CONSTRUCTION DOCUMENTS

BLM Project #
140L0621D0006


Drawn By
A.BROWN

Checked By
D.KELLEY

07 - POLE LINE ROAD
POLE LINE ROAD PLAN &
PROFILE

7CP118


P:\Projects\BLM - NV & CA\IDOT\Task Orders\Task 27 - Garnet Hill Recreation Area\Task 27 - Garnet Hill Recreation Area Title I & II Services\Engineering\Drawings\Production Drawings\07 - ROAD\208-203-07-CS.dwg 12/16/2025 8:14 AM ATANYAG

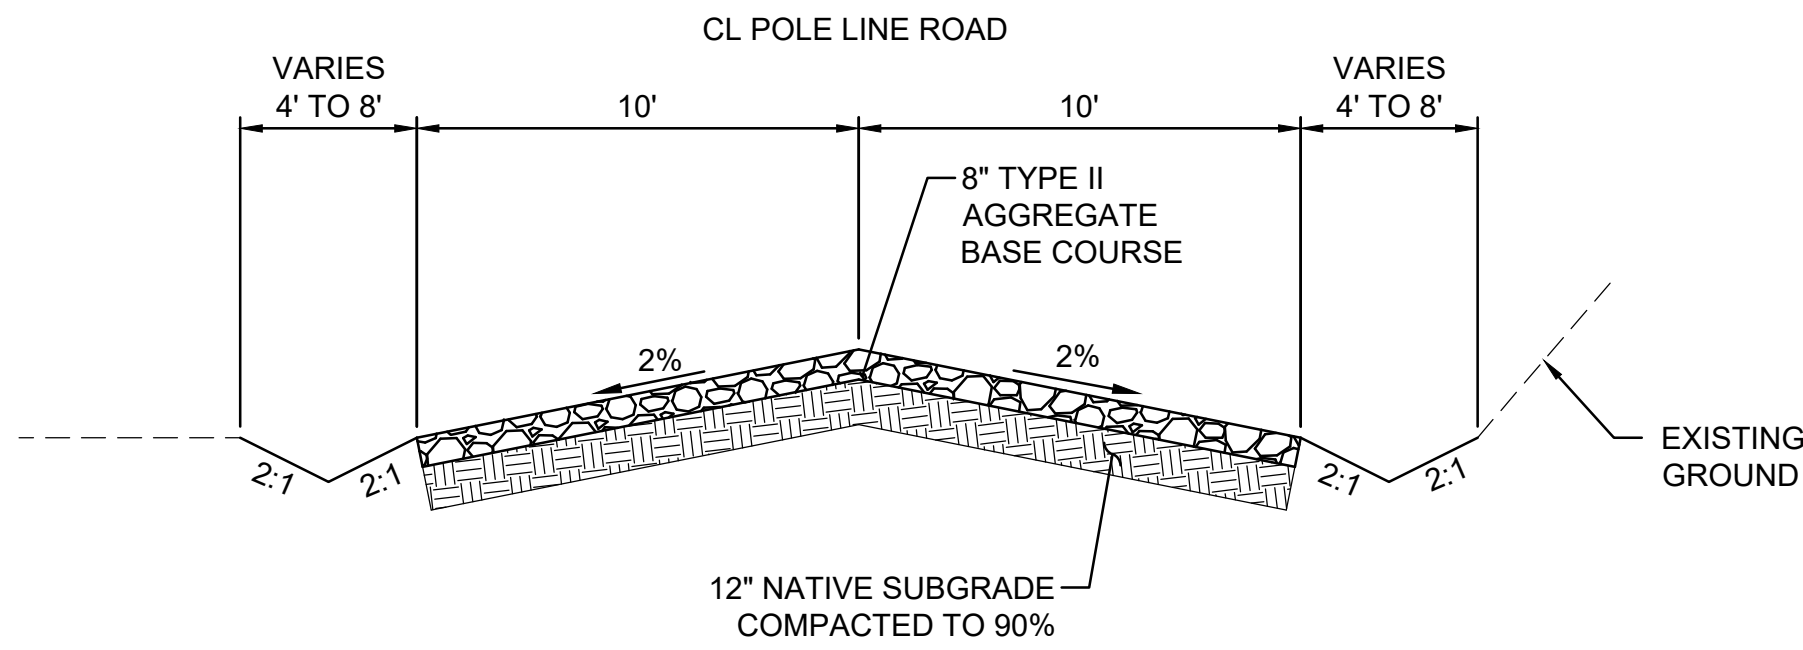

STA. 12+50.73 TO STA. 25+72.00
STA. 27+42.00 TO STA. 45+50.00
STA. 60+00.00 TO STA. 77+13.91
STA. 103+50.00 TO STA. 118+50.00
STA. 125+64.14 TO STA. 131+50.00
STA. 137+00.00 TO STA. 140+00.00
STA. 144+50.00 TO STA. 145+23.78

TYPICAL SECTION
NOT TO SCALE


1

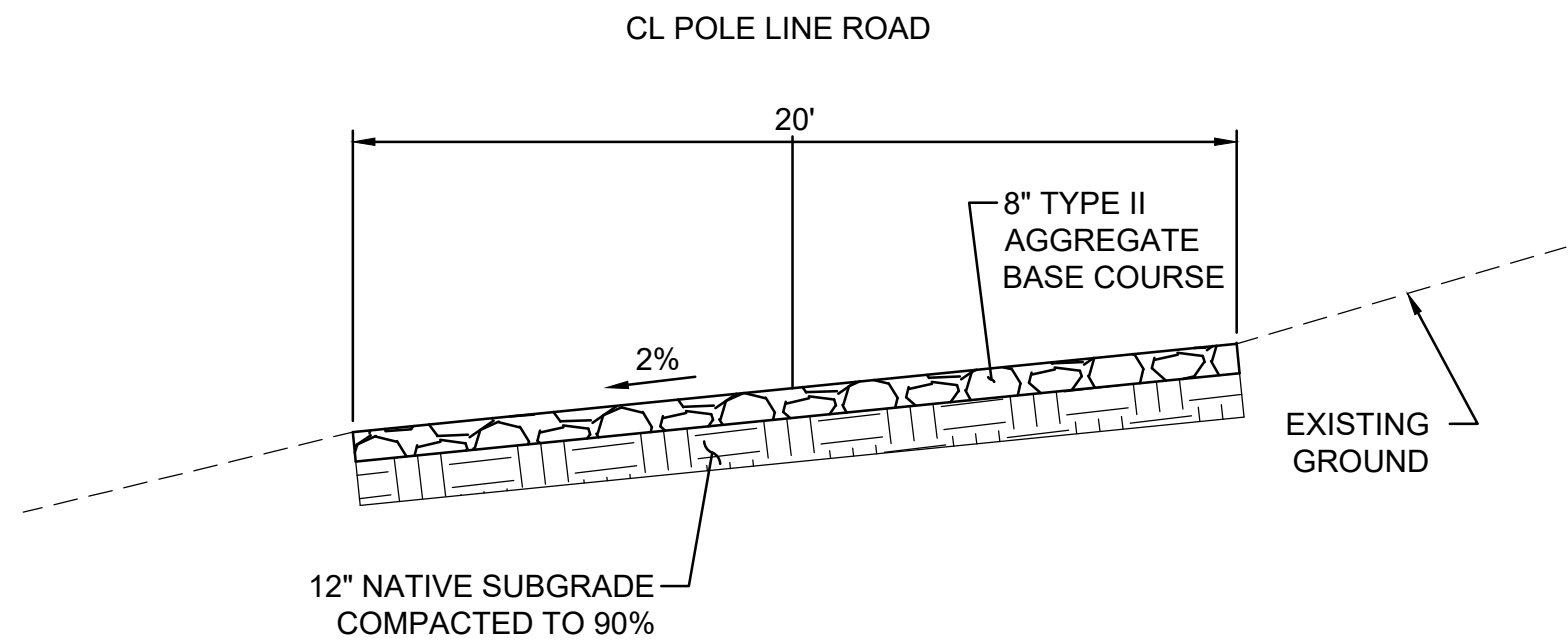

STA. 77+63.91 TO STA. 81+00.00
STA. 119+00.00 TO STA. 125+14.91

TYPICAL SECTION
NOT TO SCALE


4

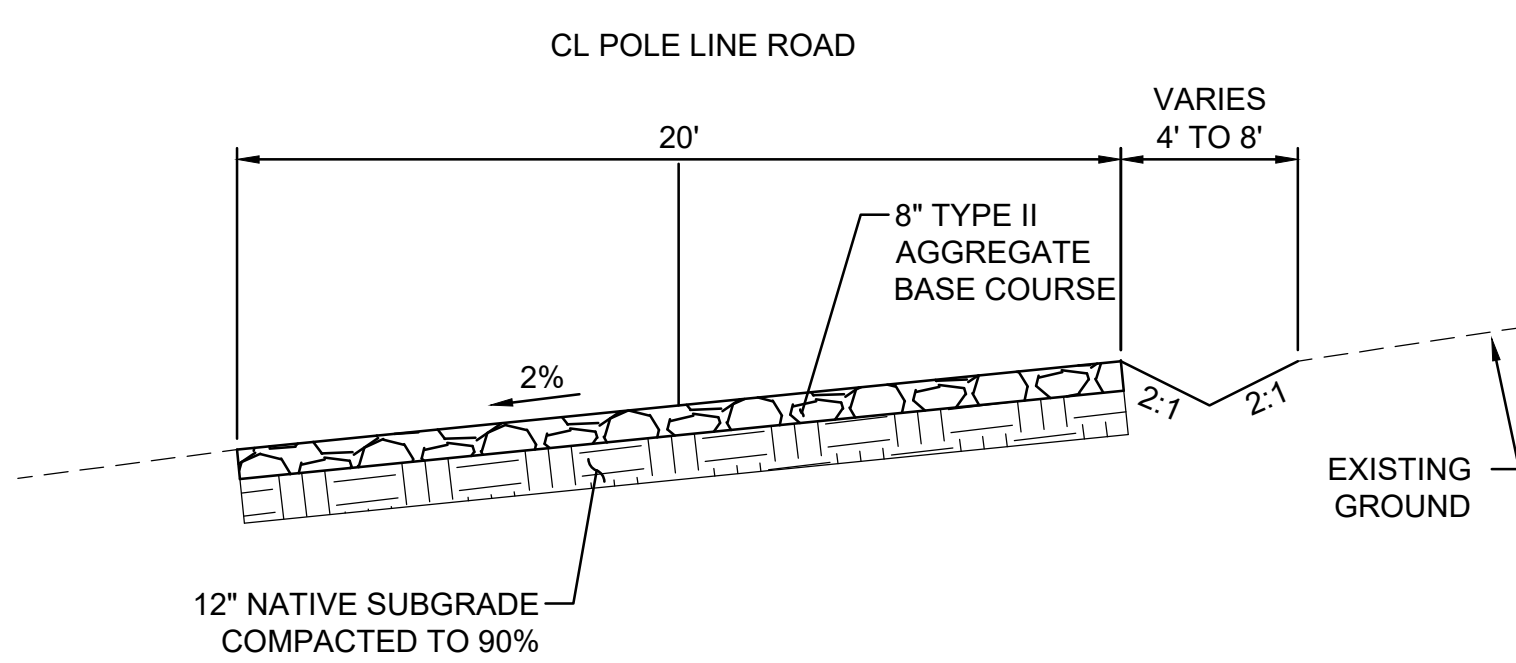

STA. 81+00.00 TO STA. 103+00.00
STA. 145+73.78 TO STA. 167+45.08

TYPICAL SECTION
NOT TO SCALE


2

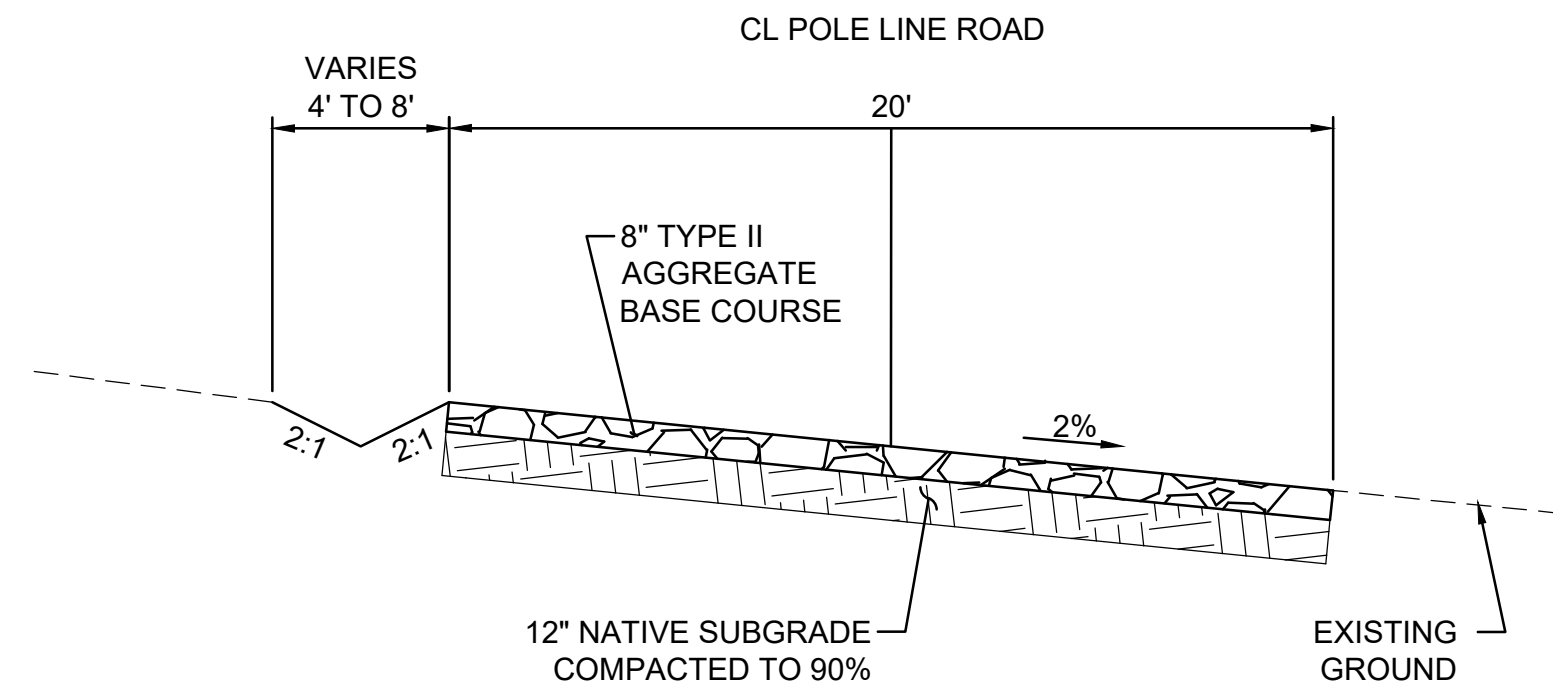

STA. 46+00.00 TO STA. 59+50.00
STA. 132+00.00 TO STA. 136+50.00
STA. 140+50.00 TO STA. 144+00.00

TYPICAL SECTION
NOT TO SCALE

3

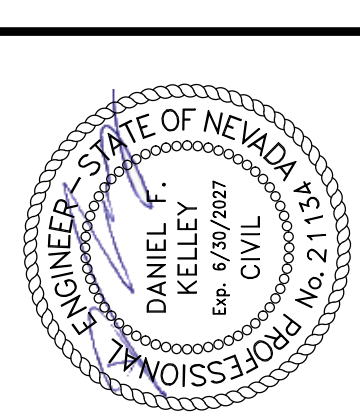

19 Dec 2025

UNITED STATES DEPARTMENT OF THE INTERIOR
BUREAU OF LAND MANAGEMENT

**GARNET HILL RECREATION AREA TITLE I
AND II SERVICES**


BUREAU OF LAND MANAGEMENT DISTRICT OFFICE
ELY, NEVADA

Project Status
100% CONSTRUCTION DOCUMENTS
BLM Project #
140L0621D0006
Drawn By
A.BROWN
Checked By
D.KELLEY





Revision Issue
Date
Description
Rev. #

07 - POLE LINE ROAD
TYPICAL SECTIONS

7CP501


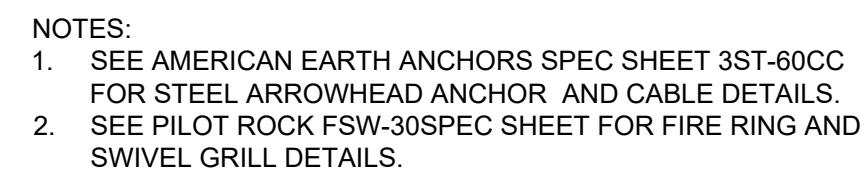


NOT TO SCALE

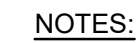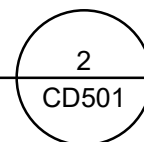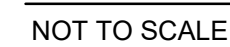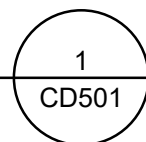

1. ALL COMPONENTS SHALL BE MINIMUM 12 GA. SQUARE POST WITH 7/16" PUNCHED THRU HOLES @ 1" ON CENTER, ON ALL FOUR SIDES. ANCHORS SHALL BE TWO PIECE BREAKAWAY ANCHORS.
2. ATTACH ANCHOR AND SLEEVE TOGETHER PRIOR TO DRIVING INTO GROUND. LEAVE AT LEAST TWO HOLES, BUT NO MORE THAN THREE HOLES ABOVE GROUND OR ABOVE SIDEWALK.
3. FOR CONCRETE INSTALLATION, DRILL A 3" TO 4" DIA. HOLE (DEPENDENT UPON ANCHOR SIZE), THE CENTER TO BE 6" FROM THE BACK OF SIDEWALK.
4. ATTACH POST TO ANCHORING SYSTEM BY USING AT LEAST TWO 3/8" DIA. DRIVE RIVETS.
5. PROVIDE 4" MINIMUM LAP BETWEEN BOTTOM OF POST AND THE BOTTOM OF THE ANCHOR/SLEEVE ASSEMBLY.
6. SIGNS LARGER THAN 24"x30" REQUIRE 3/8" x 1-1/2" FENDER WASHERS UNDER DRIVE RIVETS.
7. "U-CHANNEL" POSTS ARE NOT ACCEPTABLE.
8. BOLTS IN LIEU OF DRIVE RIVETS ARE NOT ACCEPTABLE.
9. SIGNS SHALL HAVE A STICKER AT THE BACK WITH THE NAME OF THE CONTRACTOR AND THE DATE OF INSTALLATION.
10. INSTALLATION OF SIGNS, SIGN SIZE, AND REFLECTIVITY ATTRIBUTES SHALL MEET LATEST ABA REQUIREMENTS.
11. DO NOT SET SIGN ANCHORS IN CONCRETE - CONCRETE IS TO BE DRILLED WITH HOLE REMAINING OPEN AROUND THE ANCHOR

NOT TO SCALE


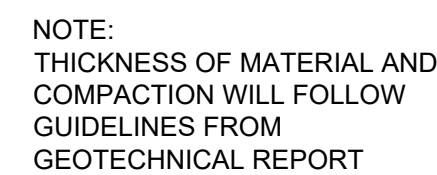
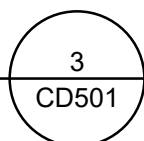


ALL GRADING AND EARTHWORK SHALL CONFORM TO THE FOLLOWING
GEOTECHNICAL REPORT:

TITLE: GEOTECHNICAL EXPLORATION REPORT
GARNET HILL RECREATION AREA-VARIOUS IMPROVEMENTS
U.S. HIGHWAY 50
NEAR ELY, NEVADA






ENGINEER: UNIVERSAL ENGINEERING SERVICES
DATE: OCTOBER 18, 2024
PROJECT NO: 4030-2400162

NOT TO SCALE

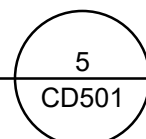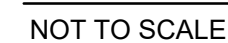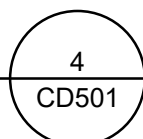

1. EPOXY COATING TO BE DARK BROWN FOR PARKING AND DRIVE AREA BOLLARDS.
2. BOLLARDS TO BE SPACED 4'-6" FROM EACH OTHER FROM CENTER TO CENTER.

NOT TO SCALE

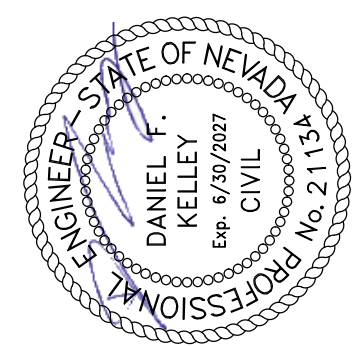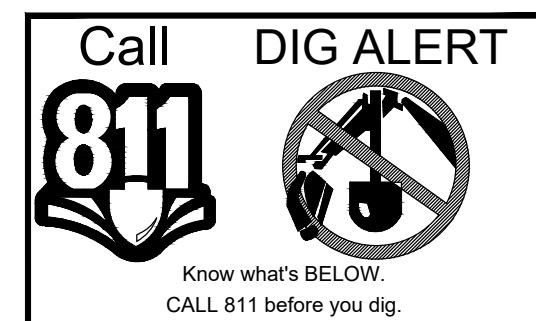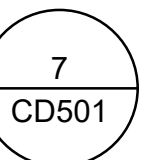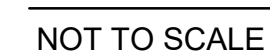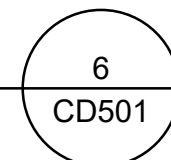

19 Dec 2025

GARNET HILL RECREATION AREA TITLE I AND II SERVICES

UNITED STATES DEPARTMENT OF THE INTERIOR
BUREAU OF LAND MANAGEMENT

BUREAU OF LAND MANAGEMENT DISTRICT OFFICE
ELY, NEVADA


Project Status	Issue Date
100%	12/19/2025
CONSTRUCTION DOCUMENTS	
BLM Project #	140L0621D0006
Drawn By	A.BROWN
Checked By	D.KELLEY

Rev. #	Description	Date
--------	-------------	------

DETAILS
CIVIL DETAILS 1

CD501

P:\Projects\BLM - NV & CA ID\Task Orders\Task 27 - Garnet Hill Recreation Area Title I & II Services\Engineering\Drawings\Production Drawings\08 - DETAILS\08-003-08-CD.dwg 12/19/2025 7:32 AM ABBROWN




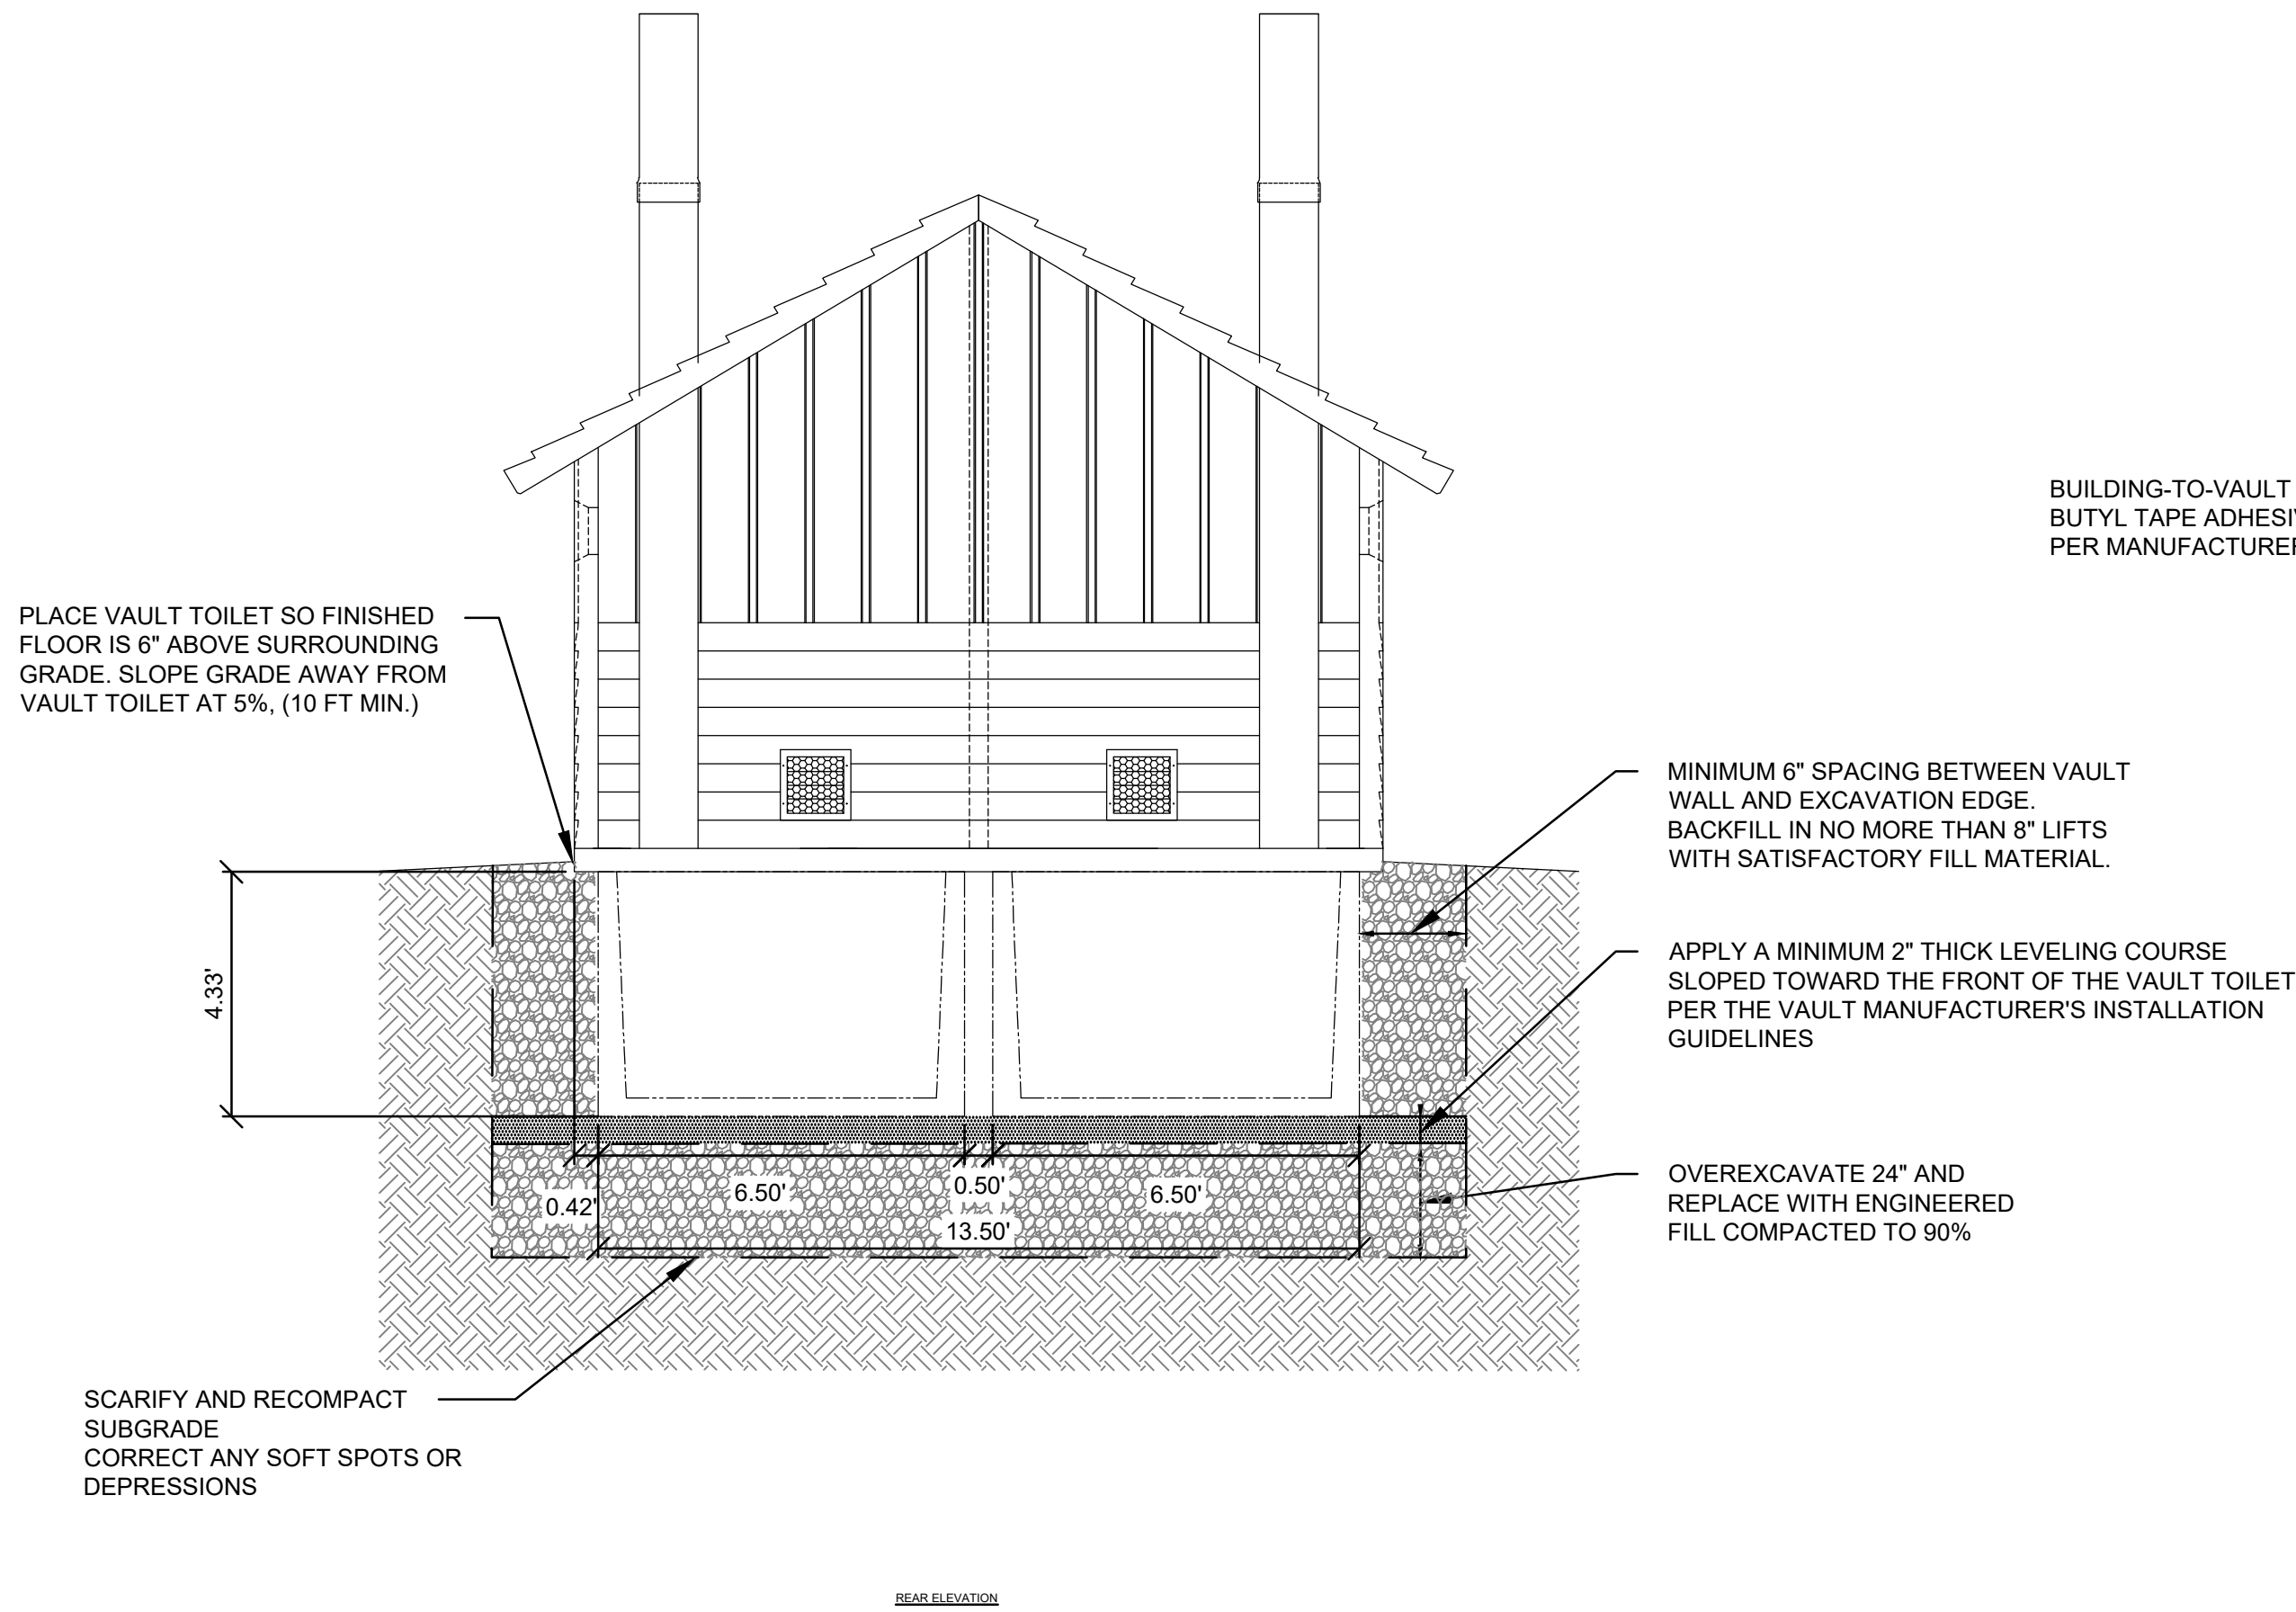


GENERAL NOTES

1. VAULT TOILET MANUFACTURER AND MODEL: CXT, DOUBLE CASCADIAN SPECIAL DIMENSIONS: 11'11\"/>

CXT DOUBLE CASCADIAN VAULT TOILET
NOT TO SCALE

1
CD502

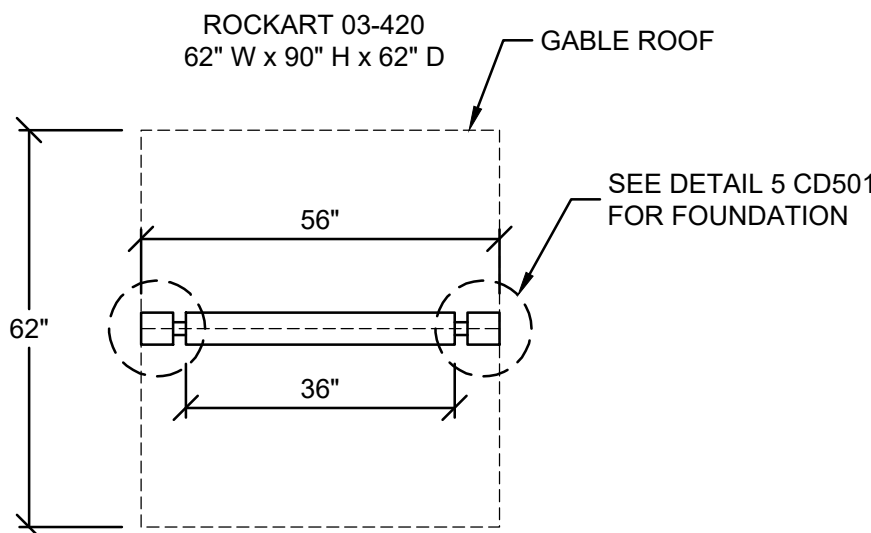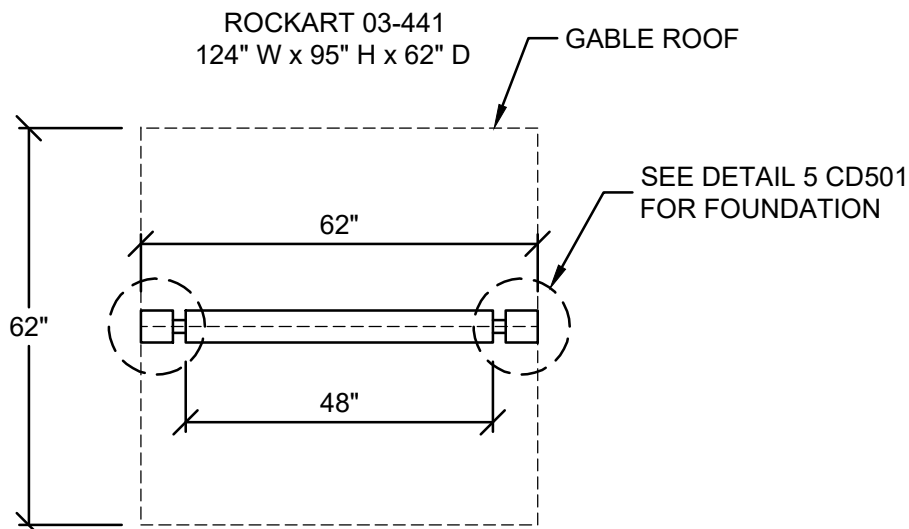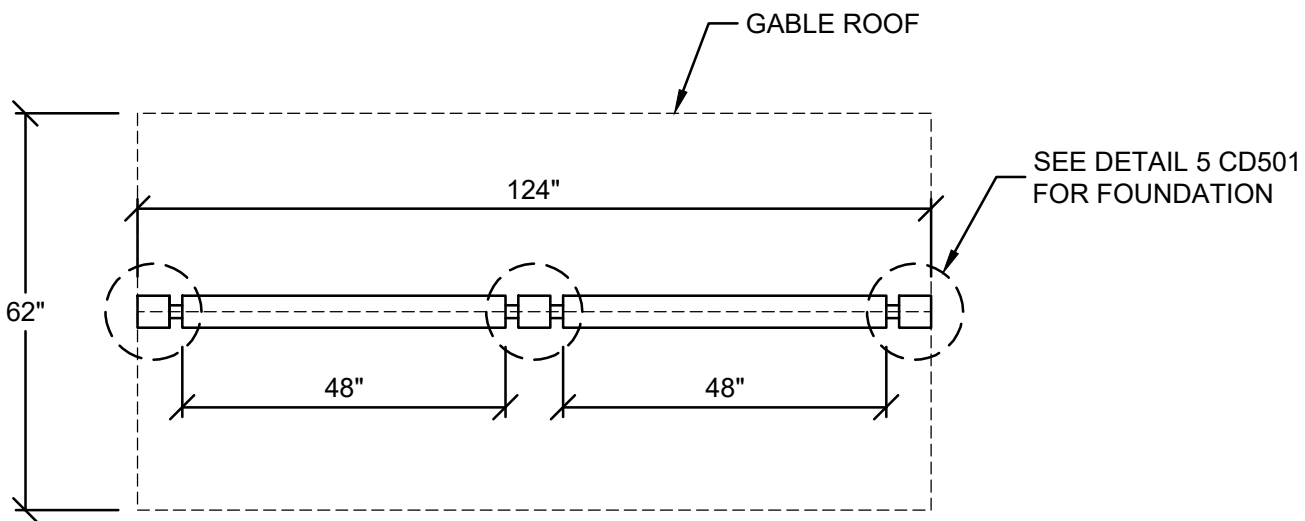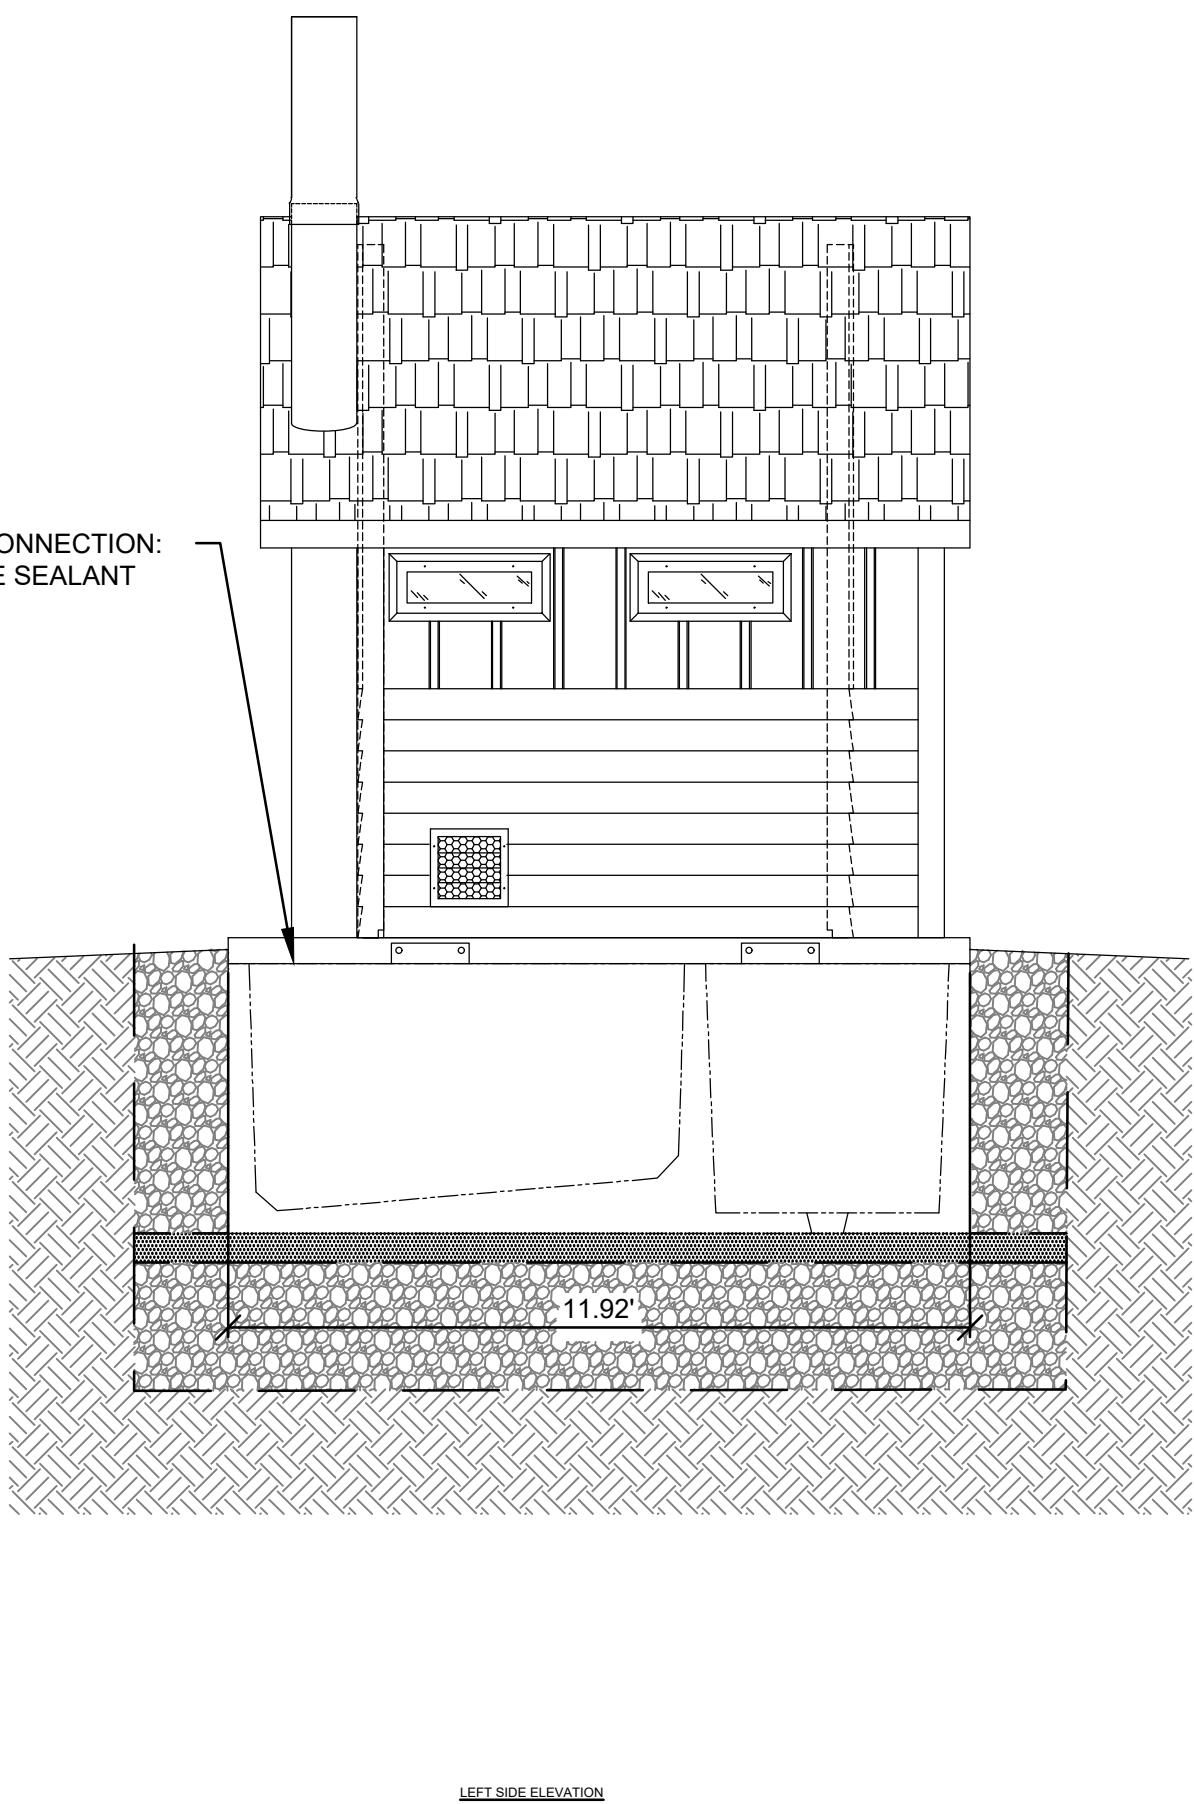


ROCKART 03-562
56\"/>

NOTES:

1. KIOSK SHALL BE ROCKART OR EQUIVALENT
2. CONTRACTOR SHALL COORDINATE WITH THE BLM FOR SIGN SPECIFICATIONS. SEE SITE PLANS 1C101-6C101 FOR SIGN CONFIGURATION.

KIOSK INSTALLATION DETAIL
NOT TO SCALE

2
CD502

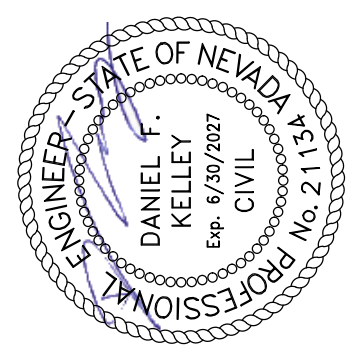

UNITED STATES DEPARTMENT OF THE INTERIOR
BUREAU OF LAND MANAGEMENT
**GARNET HILL RECREATION AREA TITLE I
AND II SERVICES**
BUREAU OF LAND MANAGEMENT DISTRICT OFFICE
ELY, NEVADA

Project Status	Issue Date
100% CONSTRUCTION DOCUMENTS	12/19/2025
BLM Project #	140L0621D0006
Drawn By	ABBROWN
Checked By	D.KELLEY


Revision Issue	Date
Description	
Rev. #	

DETAILS
CIVIL DETAILS 2

CD502

19 Dec 2025


P:\Projects\BLM - NV & CA\IDOT\Task Orders\Task 27 - Garnet Hill Recreation Area Title I & II Services\Engineering\Drawings\Production Drawings\08 - DETAILS\0208-003-08-CD.dwg 12/19/2025 7:32 AM ABBROWN

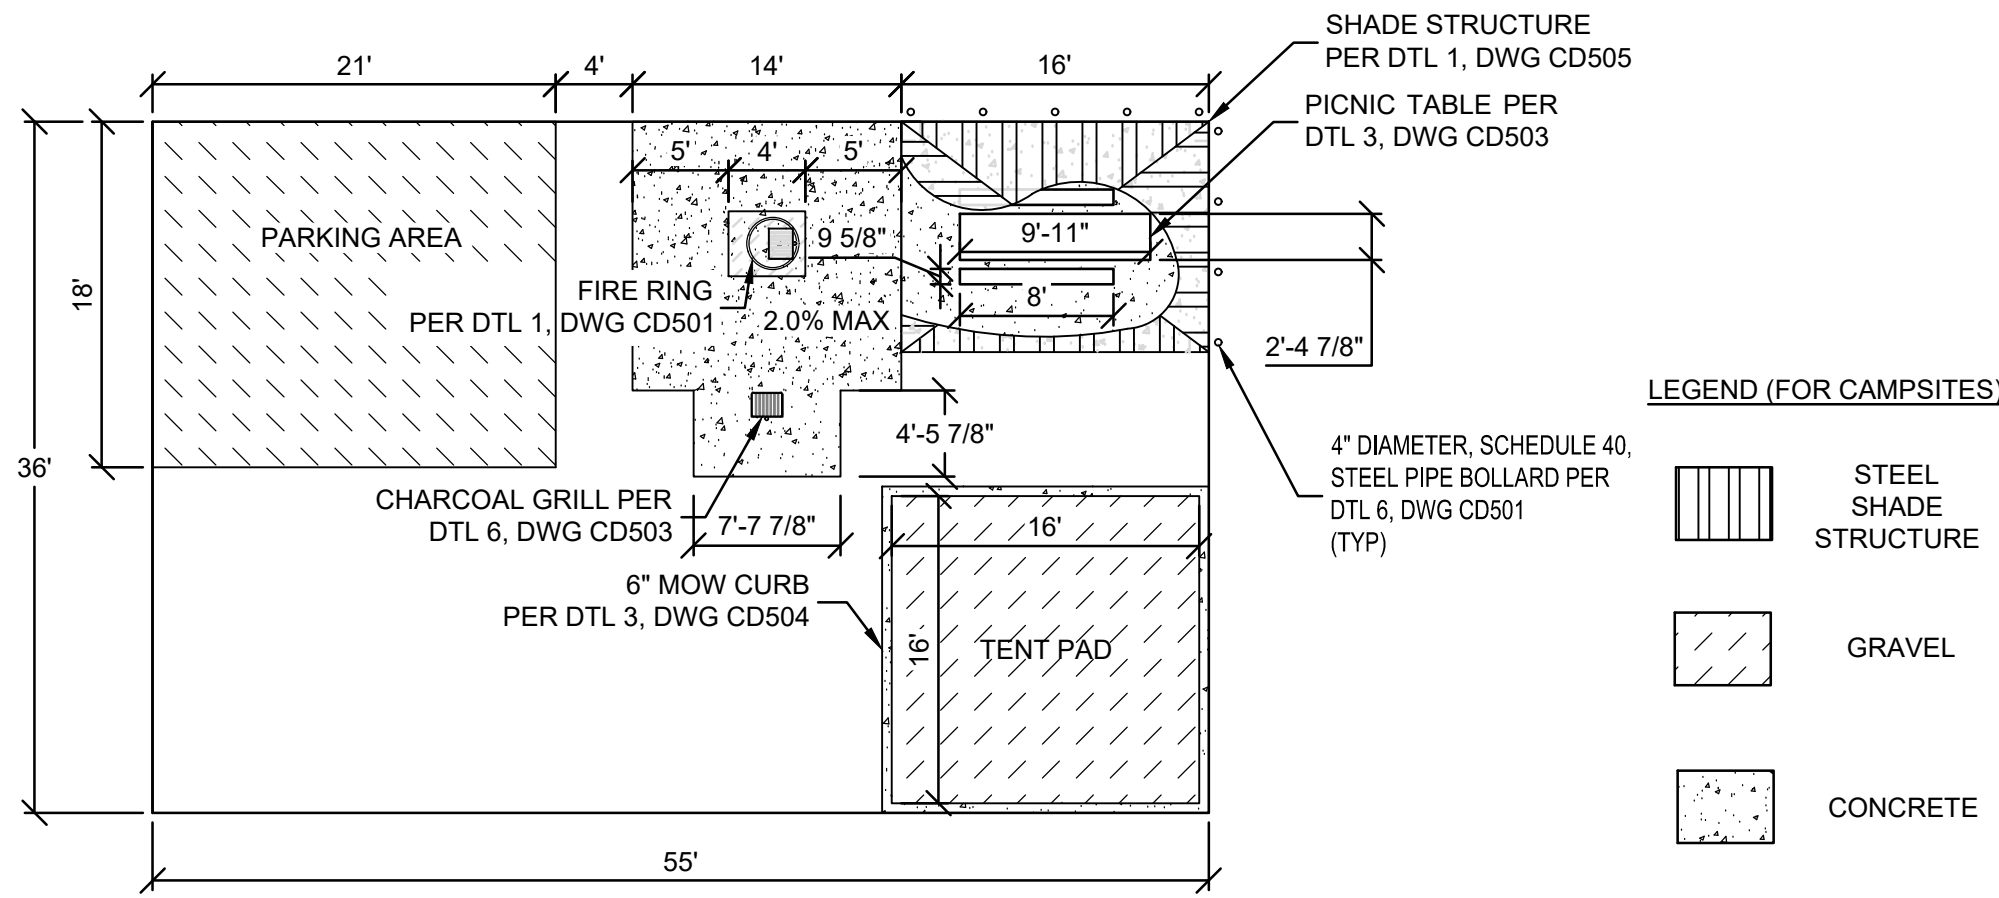

INDIVIDUAL CAMPSITE

1" = 10'


1
CD503

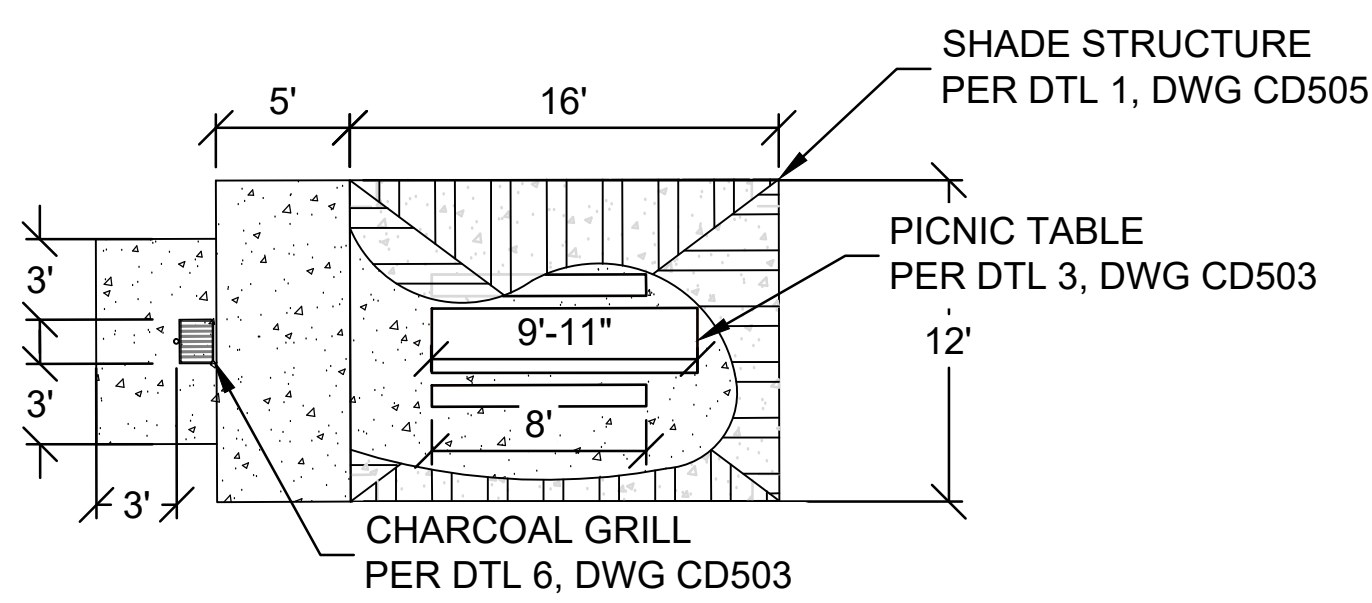

INDIVIDUAL DAY USE PICNIC SITE

NOT TO SCALE


4
CD503

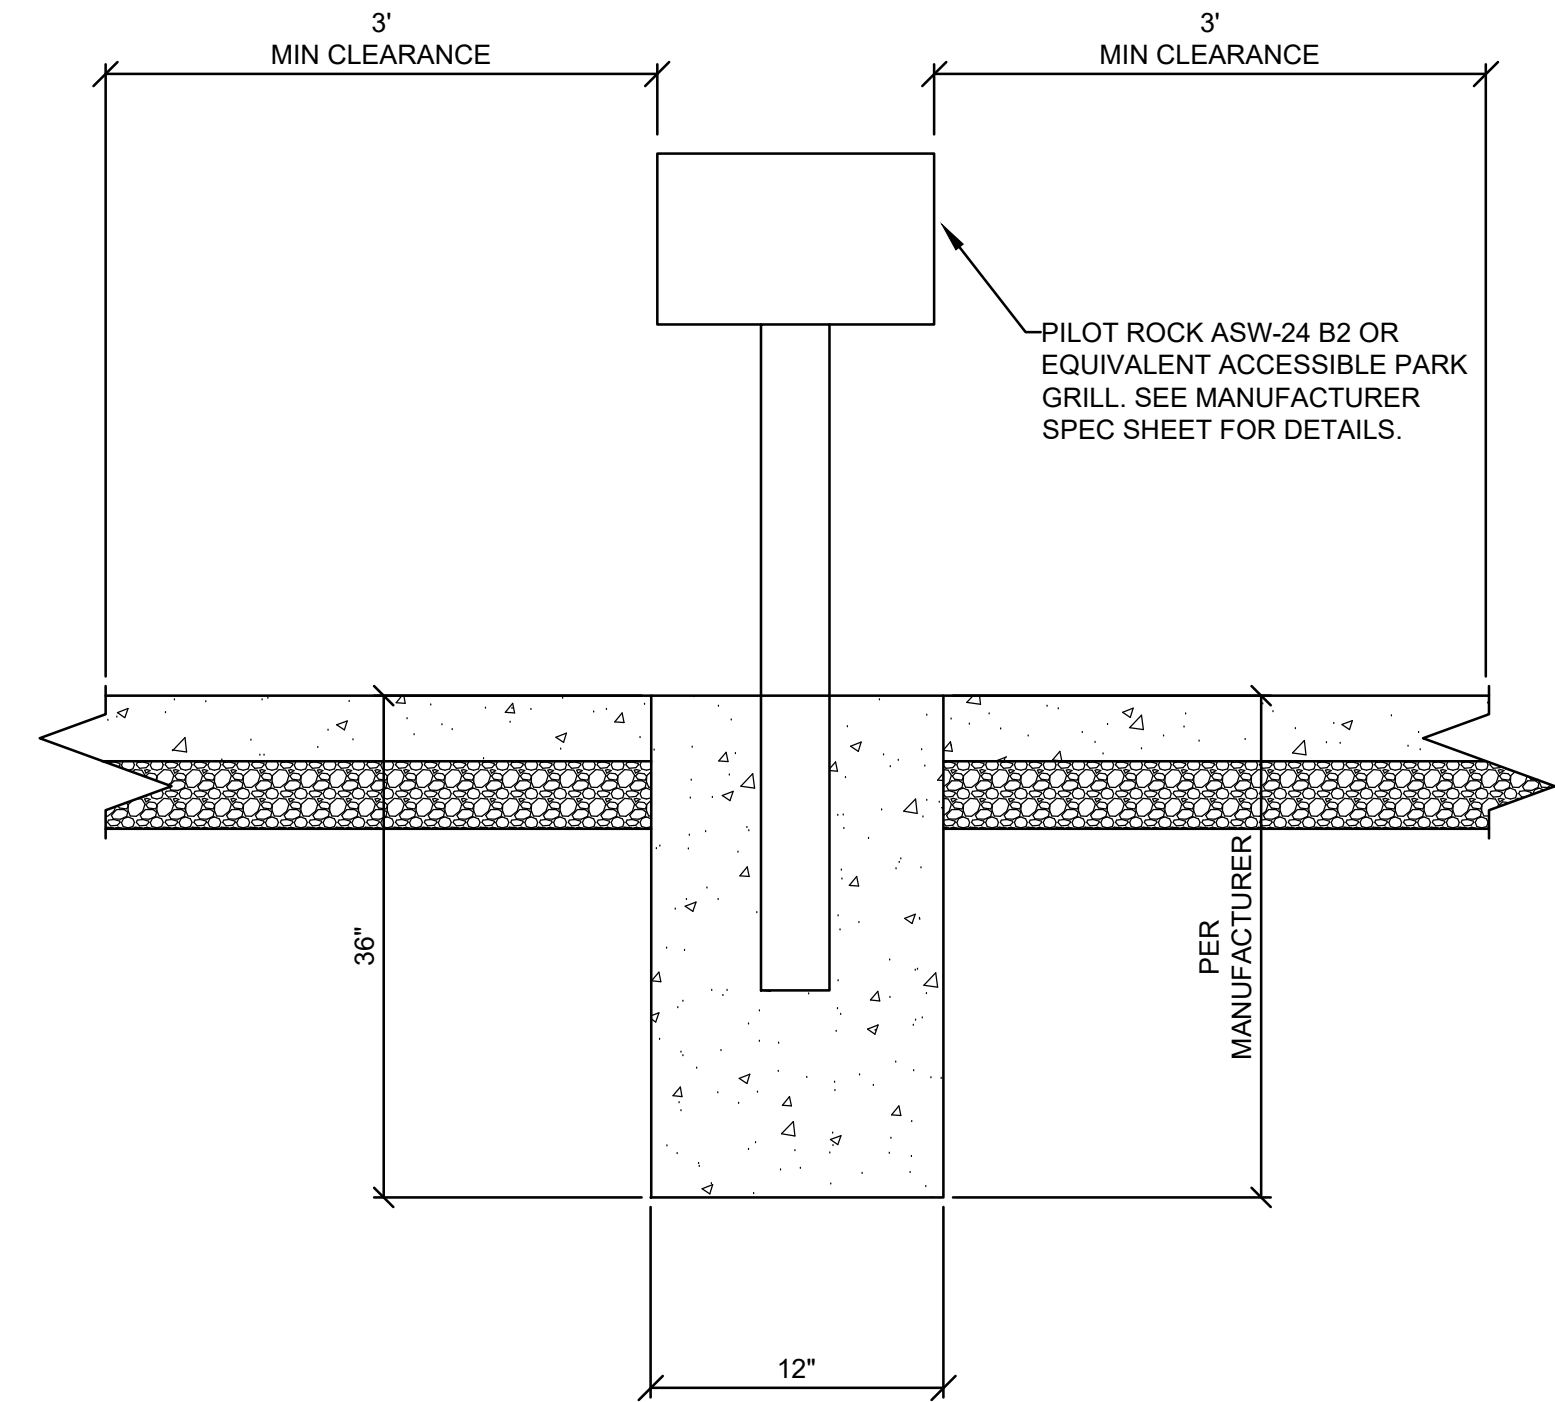

GRILL FOUNDATION DETAIL

NOT TO SCALE


6
CD503

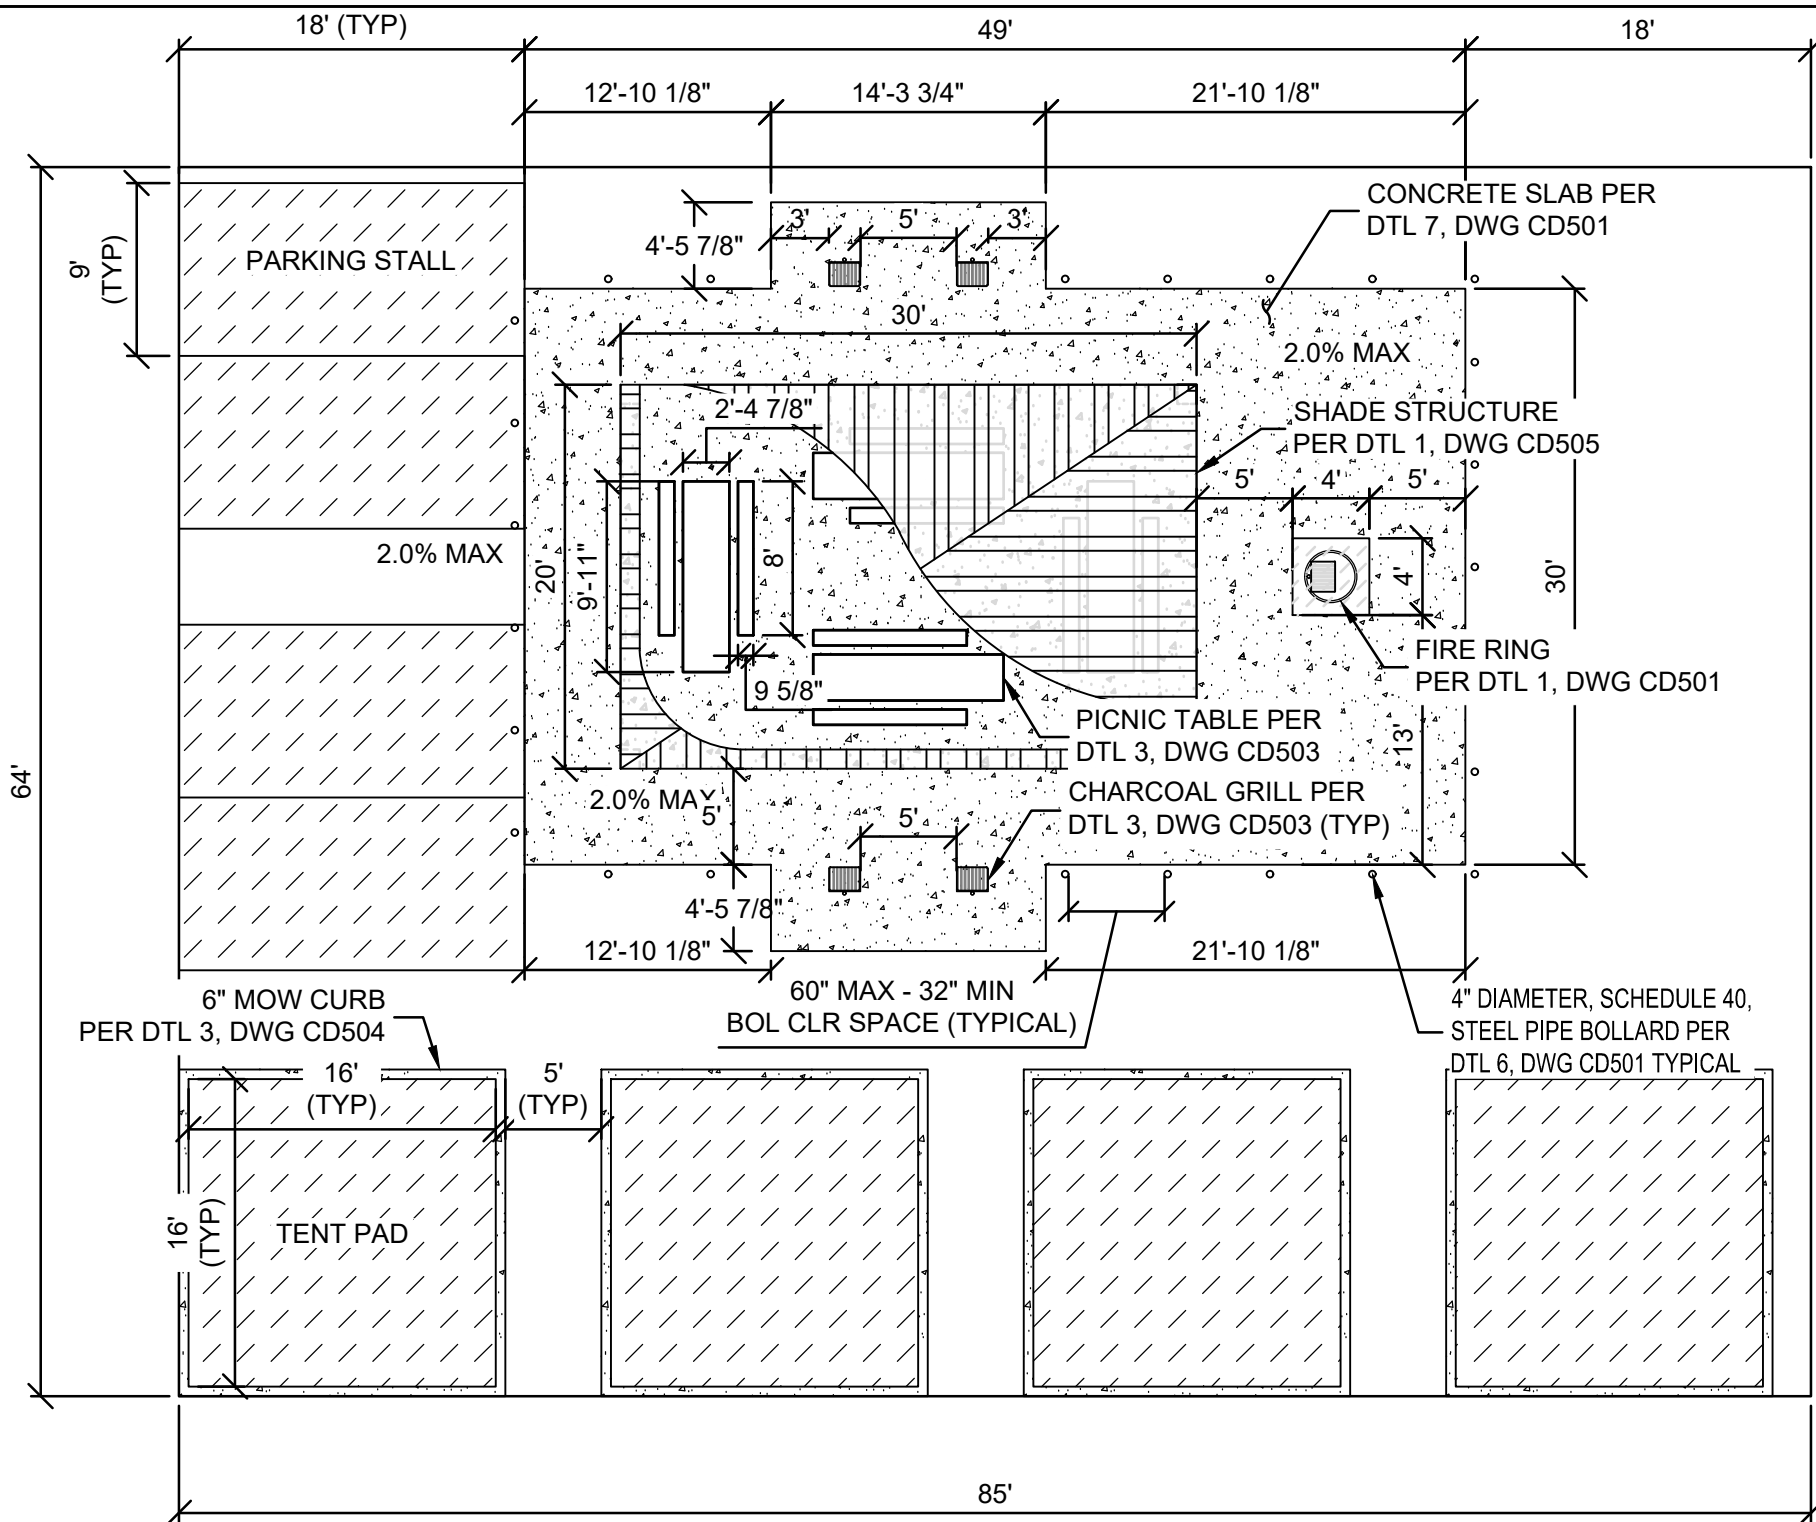

GROUP CAMPSITE

1" = 10'


2
CD503

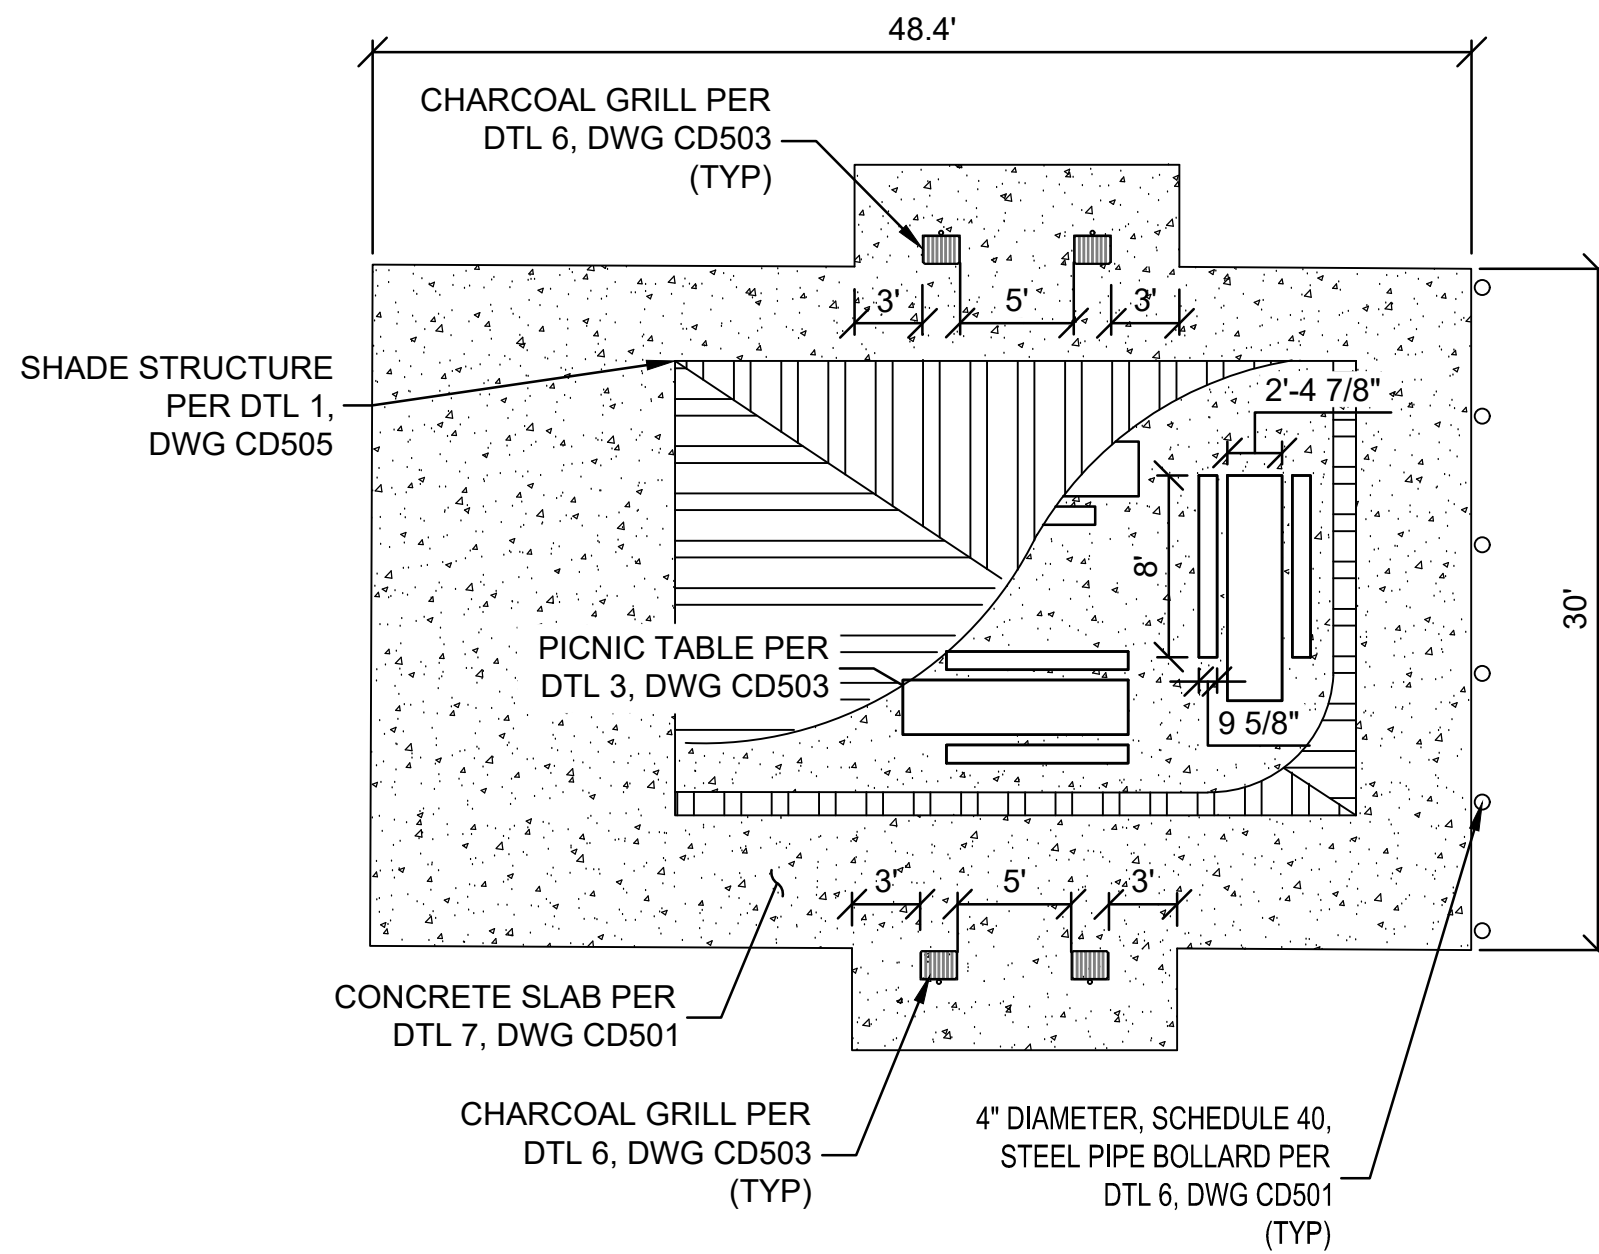

GROUP DAY USE PICNIC SITE

NOT TO SCALE



5
CD503

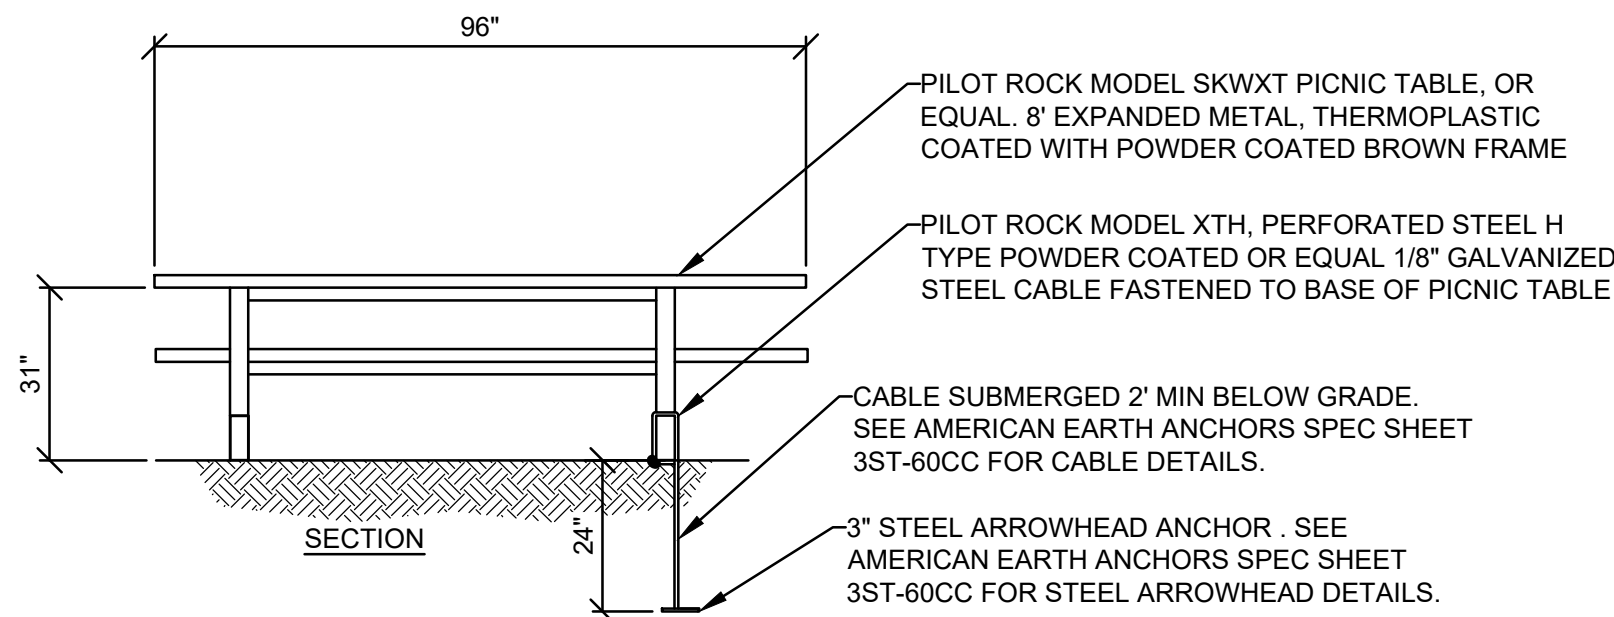

PICNIC TABLE W/ANCHOR

NOT TO SCALE

3
CD503

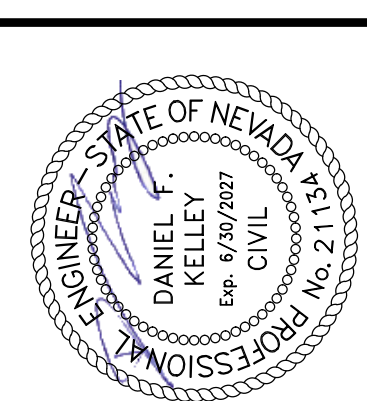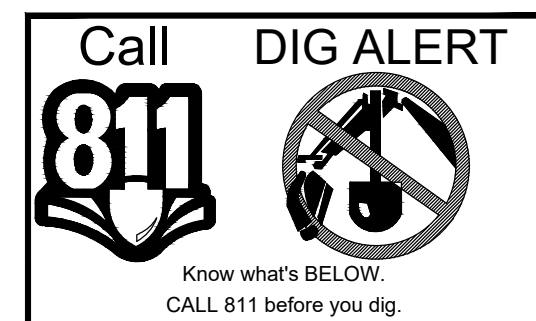

UNITED STATES DEPARTMENT OF THE INTERIOR
BUREAU OF LAND MANAGEMENT

**GARNET HILL RECREATION AREA TITLE I
AND II SERVICES**

BUREAU OF LAND MANAGEMENT DISTRICT OFFICE
ELY, NEVADA

Issue Date
12/19/2025

Project Status
100% CONSTRUCTION DOCUMENTS

BLM Project #
140L0621D0006

Drawn By
ABBROWN

Checked By
D.KELLEY

Revision Issue
Description

Rev.
#

DETAILS
CIVIL DETAILS 3

CD503

