


VETERANS AFFAIRS MEDICAL CENTER

500 E VETERANS ST
TOMAH, WI 54660

CONNECT B406 AHU'S TO EMERGENCY POWER

PROJECT NO.: 676-22-108

CAMPUS MAP

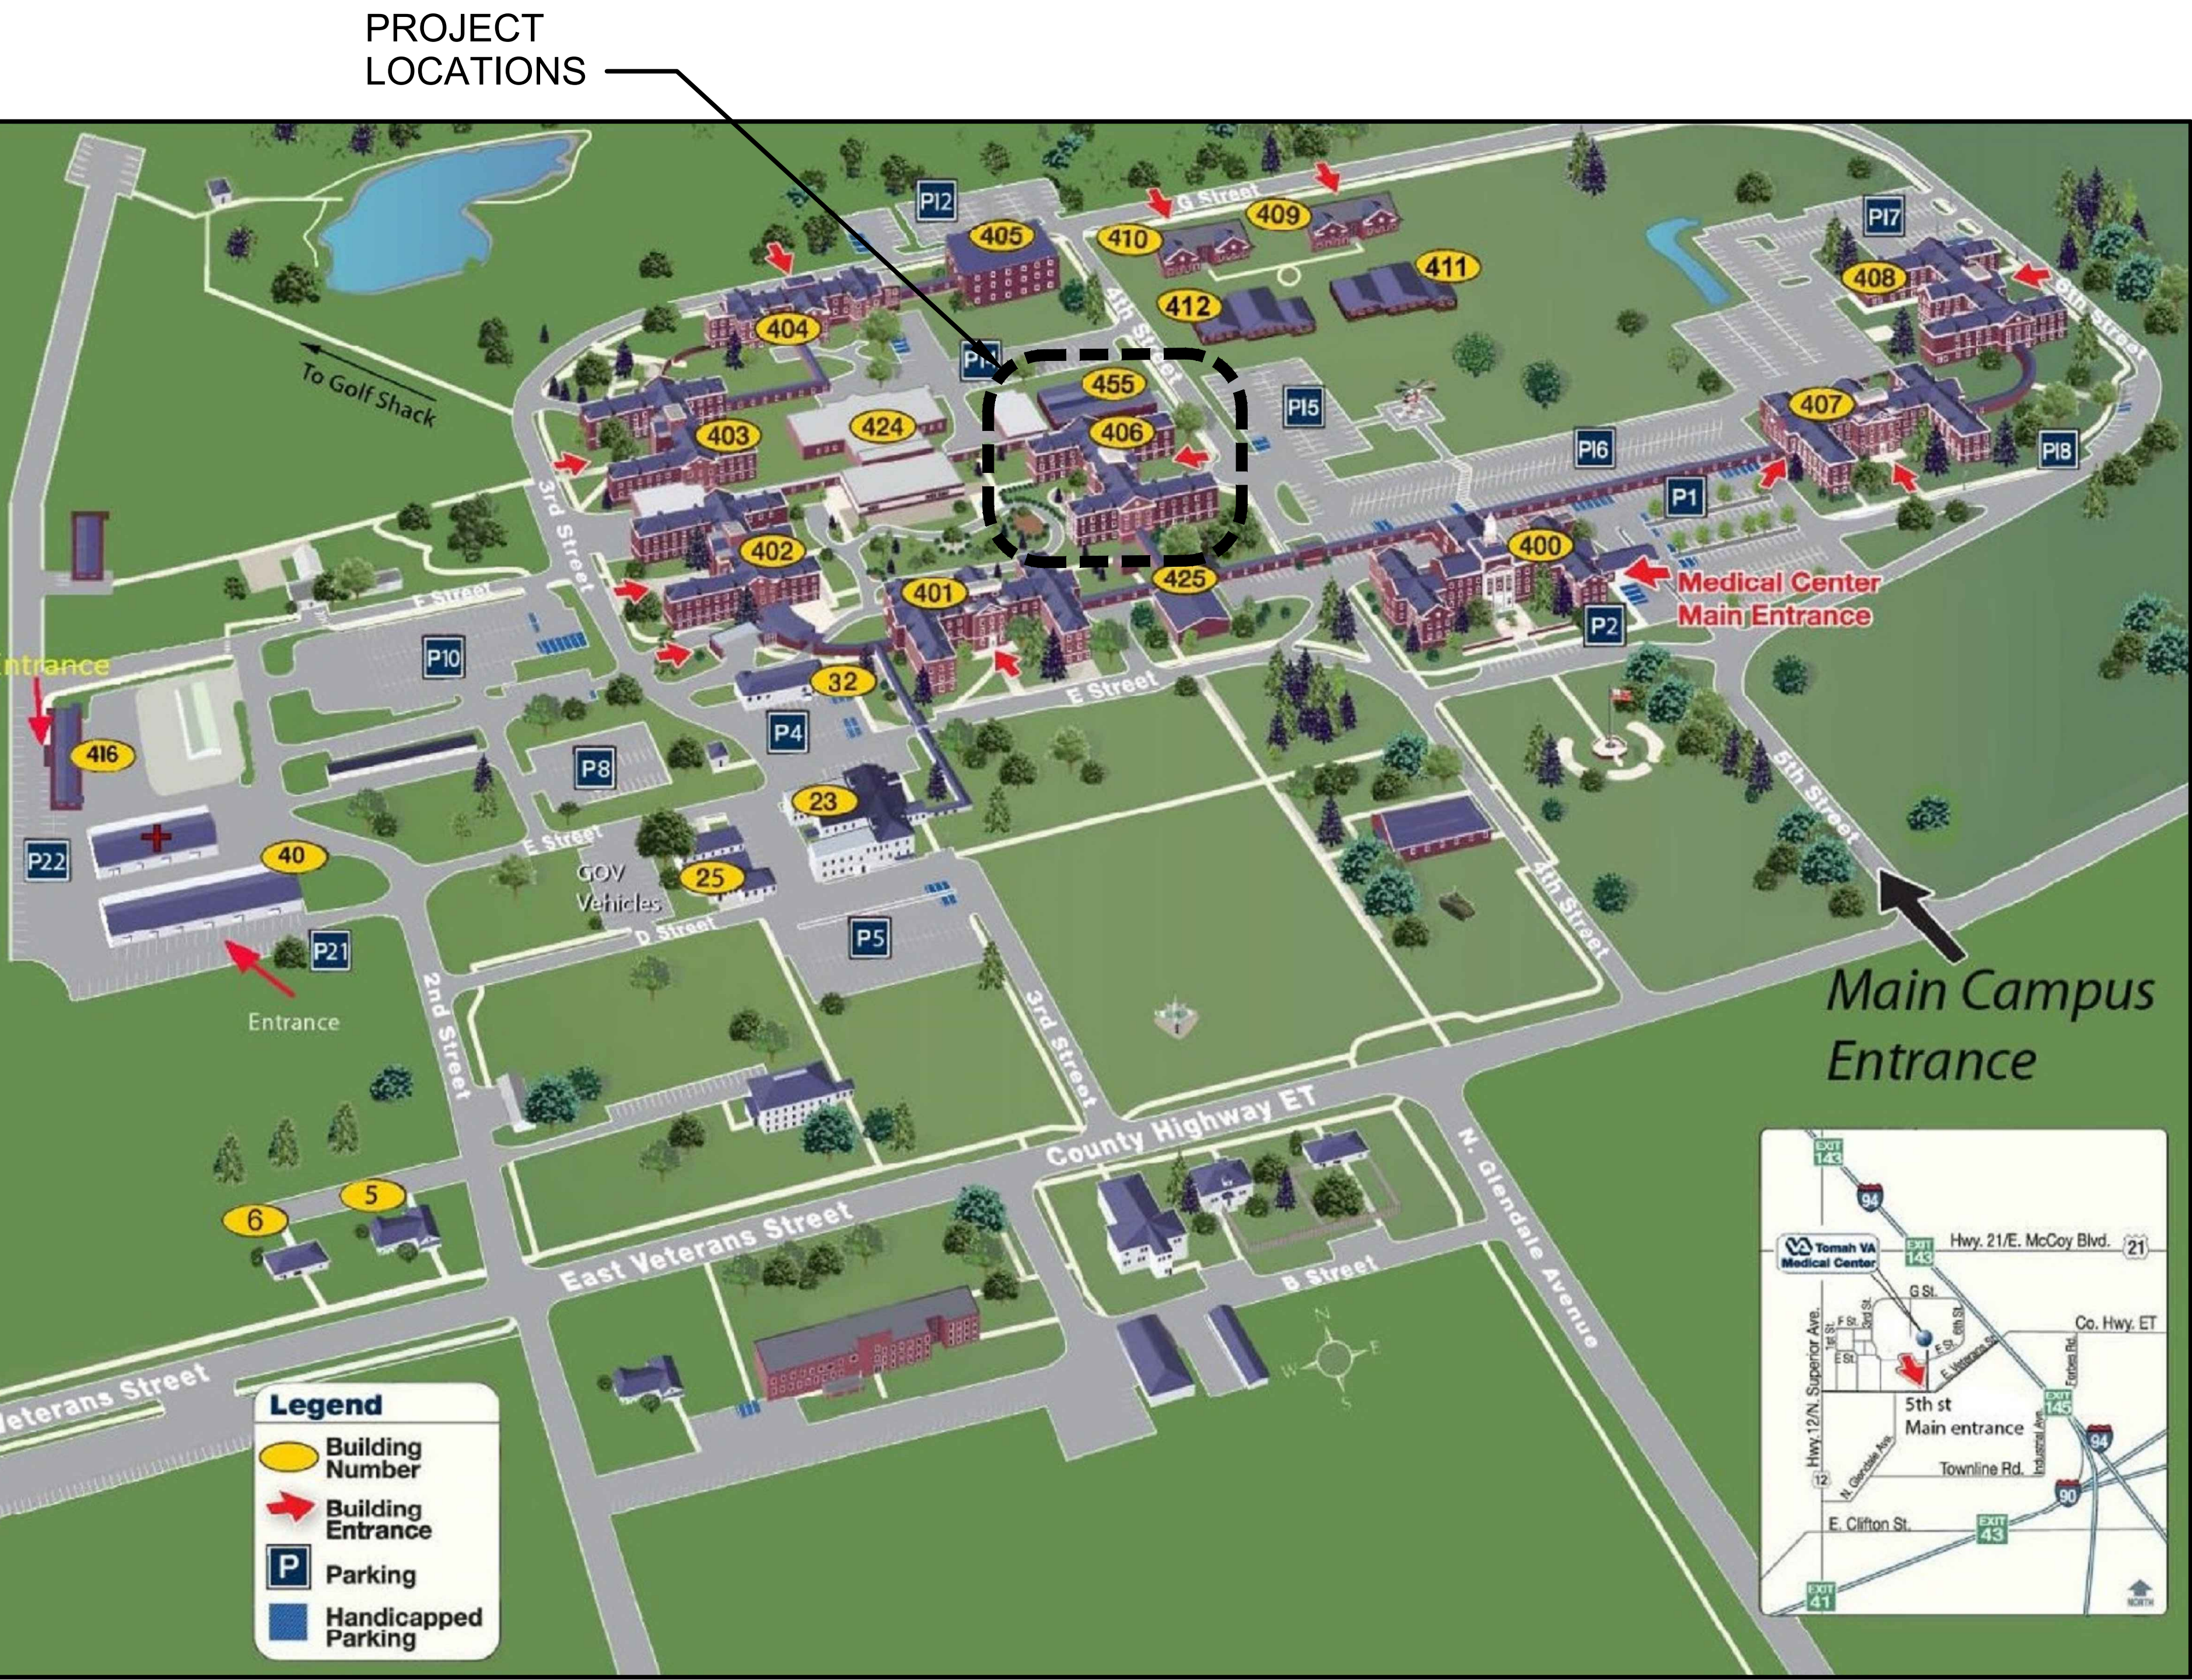

SITE PLAN



PROJECT TEAM

PROJECT LEADER / ARCHITECT

PENN CONSTRUCTION GROUP

1021 N. Superior
Unit 11
Tomah, Wisconsin 54660

MECHANICAL

PENN CONSTRUCTION GROUP

1021 N. Superior
Unit 11
Tomah, Wisconsin 54660

PLUMBING

PENN CONSTRUCTION GROUP

1021 N. Superior
Unit 11
Tomah, Wisconsin 54660

ELECTRICAL

PENN CONSTRUCTION GROUP


1021 N. Superior
Unit 11
Tomah, Wisconsin 54660

SHEET INDEX

SHEET NUMBER	SHEET NAME	ISSUED FOR 35% SD 9/02/2025	RE-ISSUED FOR 35% SD 9/22/2025	ISSUED FOR 65% DD 10/31/2025	ISSUED FOR 95% CD 11/14/2025	ISSUED FOR BID 11/20/2025
GENERAL INFORMATION						
G001	TITLE SHEET	X	X*	X	X	X
GC101	LIFE SAFETY PLAN	X	X	X	X	X
GC102	INFECTION CONTROL PLANS	X	X	X	X	X
GC103	PHASING PLAN	X	X	X	X	X
CIVIL						
C001	LEGEND AND GENERAL NOTES	X	X	X	X	X
CD101	PARTIAL SITE AND WORK AREA SITE PLANS - DEMOLITION	X	X	X	X	X
C101	PARTIAL SITE AND WORK AREA SITE PLANS - NEW WORK	X	X	X	X	X
C501	DETAILS	X	X	X	X	X
HAZARDOUS						
HA101	HAZARDOUS MATERIALS OVER-ALL FLOOR PLAN					X
ARCHITECTURAL						
A001	LEGENDS, ABBREVIATIONS, AND NOTES	X	X	X	X	X
A101	B446/B406 PARTIAL FIRST FLOOR PLANS - NEW WORK	X	X	X	X	X
MECHANICAL						
M001	LEGENDS, ABBREVIATIONS, AND NOTES	X	X	X	X	X
MH101	B446 FIRST FLOOR PLAN AND SCHEDULE - NEW WORK	X	X	X	X	X
M501	DETAILS & DIAGRAMS	X	X	X	X	X
ELECTRICAL						
E001	SYMBOLS AND ABBREVIATIONS	X	X*	X	X	X
ED101	B406 UTILITY TUNNEL UNDERGROUND PLAN - DEMOLITION	X	X*	X	X	X
ED102	B406 PARTIAL CRAWLSPACE PLAN - DEMOLITION	X	X*	X	X	X
ED103	B446/B406 PARTIAL FIRST FLOOR PLAN - DEMOLITION			X	X	X
ED601	ONE-LINE DIAGRAM - DEMOLITION			X	X	X
EP101	B406 UTILITY TUNNEL UNDERGROUND PLAN - NEW WORK	X	X*	X	X	X
EP102	B406 PARTIAL CRAWLSPACE PLAN - NEW WORK	X	X*	X	X	X
EP103	B446 FIRST FLOOR AND SECTIONS - NEW WORK			X	X	X
E401	SECTIONS			X	X	X
E501	DETAILS & DIAGRAMS	X	X*	X	X	X
E601	ONE-LINE DIAGRAM - NEW WORK	X	X*	X	X	X
E602	ELECTRICAL SCHEDULES	X	X*	X	X	X

* INDICATES DRAWING UPDATED OCTOBER 15, 2025

14 NOTE: SEE CIVIL AND ELECTRICAL DRAWINGS FOR ADDITIONAL SITE INFORMATION

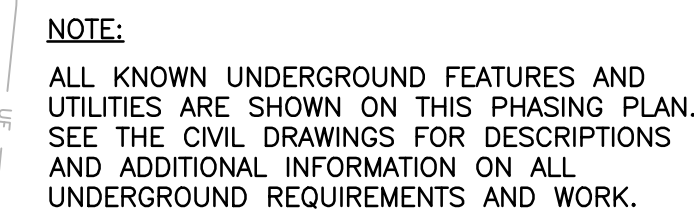

$$1/4'' = 1' - 0''$$


Drawing Number

A
three inches = one foot
1
one and one half inches = one foot
2
one inch = one foot
3
three quarters inch = one foot
4
one half inch = one foot
5
three eighths inch = one foot
6
one eighth inch = one foot
7
one quarter inch = one foot
8
one eighth inch = one foot
9
one eighth inch = one foot

GENERAL NOTES:

1. CONTRACTOR SHALL ADHERE STRICTLY TO STATE AND FEDERAL OCCUPATIONAL SAFETY AND HEALTH ADMINISTRATION (OSHA) STANDARDS. A MINIMUM OF 10-HOUR OSHA TRAINING IS REQUIRED FOR ALL CONTRACT WORKERS ON SITE. TRAINING MUST BE CURRENT WITHIN THE LAST TWO YEARS.
2. CONTRACTOR SHALL PROVIDE WRITTEN CERTIFICATION THAT ALL CONTRACT WORKERS ON SITE HAVE BEEN SCREENED FOR TUBERCULOSIS WITHIN 90 DAYS PRIOR TO ASSIGNMENT TO THE WORK SITE AND HAVE BEEN FOUND TO HAVE NEGATIVE SCREENING REACTIONS.
3. ALL HOT WORK PERMITS MUST BE OBTAINED FROM THE VA FIRE DEPARTMENT. PERMIT IS VALID FOR ONE WEEK.
4. ALL DISTURBED GRASS SHALL BE RE-SODDED AT END OF THE CONSTRUCTION. ALL DAMAGED LAWN WILL BE OVERCUT BY 6" OR MORE TO ACCOMMODATE FULL WIDTH ROLLS OF SOD. CONTRACTOR SHALL PROVIDE 3" BROWN SIFTED TOPSOIL, TOPSOIL TO BE TILLED AND GRADED TO A SMOOTH MATCHING GRADE OF UNDAMAGED LAWN. SLOPE NEW GRADE AWAY FROM BUILDING 1A. SOD TO BE THOROUGHLY SATURATED WITH WATER UPON PLACEMENT. THE CONTRACTOR IS RESPONSIBLE FOR WATERING NEW SOD UNTIL PROJECT ACCEPTANCE BY THE COR.
5. CONSTRUCTION STAGING (LIMITS OF CONSTRUCTION) AREA SHALL BE COMPLETELY FENCED IN AND LOCKED DURING OFF HOURS. ADDITIONAL SPACE IF REQUIRED SHALL BE COORDINATED WITH THE VA CONSTRUCTION MANAGER.
6. THE CONTRACTOR SHALL PROVIDE PORTABLE RESTROOM FACILITIES FOR ALL CONTRACTOR AND SUB-CONTRACTORS USE THROUGHOUT THE DURATION OF THE PROJECT. FACILITY RESTROOM USE IS NOT ALLOWED BY ANY CONSTRUCTION PERSONNEL.
7. ALL CONSTRUCTION AREAS SHALL BE CLEANED DAILY.
8. ALL CONTRACTOR AND SUB-CONTRACTOR VEHICLES SHALL PARK IN THE DESIGNATED AREA.
9. ONE CONSTRUCTION TRAILER MAY BE PARKED IN THE DESIGNATED AREA PROVIDED BY THE VA. ELECTRICAL HOOK UP SHALL BE THE CONTRACTORS RESPONSIBILITY AND COORDINATED WITH THE VA CONSTRUCTION MANAGER. EACH CONNECTION SHALL BE METERED INDIVIDUALLY.
10. NO SANITARY OR WATER CONNECTIONS ALLOWED.
11. CONTRACTOR SHALL REPAIR ALL ROADWAY DAMAGED FROM CONSTRUCTION TO MATCH EXISTING CONDITIONS. RECORD EXISTING CONDITIONS BY DATED PHOTOGRAPH OF SITE.
12. CONTRACTOR TO ENSURE ALL FIRE HYDRANTS AROUND BUILDING ARE NOT BLOCKED OFF OR UNUSABLE.
13. THE CONTRACTOR SHALL VERIFY ALL DIMENSIONS IN THE FIELD BEFORE STARTING CONSTRUCTION. THE CONTRACTOR SHALL BE RESPONSIBLE FOR ALL FIELD DIMENSIONS. IF ANY DISCREPANCIES ARE FOUND IN THESE PLANS FROM ACTUAL CONDITIONS, THE CONTRACTOR SHALL NOTIFY THE VA AND A/E IMMEDIATELY.
14. THE UNDERGROUND UTILITY INFORMATION AS SHOWN HEREON IS BASED, UPON INFORMATION COLLECTED ON OCTOBER 31, 2025. WHILE THIS INFORMATION IS BELIEVED TO BE RELIABLE, ITS ACCURACY AND COMPLETENESS CANNOT BE GUARANTEED OR CERTIFIED. GO TO PROVIDE VERIFICATION UTILITY LOCATING PRIOR TO ANY EARTH WORK.

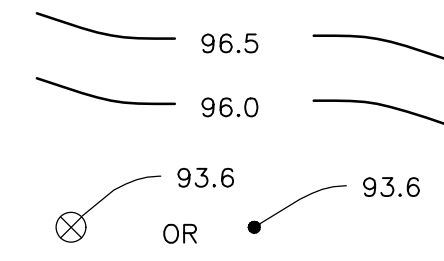


- EXISTING ROADS TO REMAIN
- CATCH BASIN, STORMWATER INLET
- MANHOLE
- ELECTRICAL MANHOLE
- ELECTRICAL HANDHOLE
- AREA-LIGHTING BASE
- SURVEY BASE LINE MONUMENT
- POINT OF INTERSECTION
- SURFACE ELEVATION
- DRAINAGE WAY OR DITCH
- DRAWING MATCH LINE
- CENTERLINE, BUILDING, ROAD, ETC.
- STAGING, STOCKPILE, AND PLAN HOLDING AREA LIMITS
- REMODELED EXISTING PLANT STRUCTURE
- NEW STRUCTURE-THIS CONTRACT PROPOSED STRUCTURE
- STRUCTURE NUMBER
- EXISTING TREES TO REMAIN
- POWER POLE WITH GUY SUPPORT
- RELOCATED OVERHEAD POWER LINE
- UNDERGROUND TELEPHONE LINE
- GATE (SHOWN WITH FENCE TYPES ABOVE)
- EXISTING GRADE
- FINISH GRADE
- PI (POINT OF INTERSECTION)
- VPI (VERTICAL POINT OF INTERSECTION) AND
- RADIAL POINT
- TEST PIT
- BORING LOCATION AND NUMBER
- PIEZOMETER
- EXISTING UTILITY OR TELEPHONE POLE
- NEW UTILITY OR TELEPHONE POLE
- DI (DROP INLET)
- LIGHT STANDARD

LEGEND

- EXISTING STRUCTURE
- EXISTING AC PAVEMENT
- NEW AC PAVEMENT
- GRAVEL SHOULDER
- CONCRETE WALK
- DRAINAGE DITCH
- ROAD
- RAILROAD TRACKS
- PROPERTY LINE
- RIGHT-OF-WAY LINE
- EASEMENTS LINE
- CENTER LINE, BUILDING, ROAD, ETC.
- SURVEY REFERENCE LINE
- FENCE
- CONNECT TO EXISTING
- NATURAL GAS LINE
- WATER LINE
- STORM SEWER LINE
- SANITARY SEWER LINE
- UNDERGROUND ELECTRIC
- COMMUNICATIONS LINE
- TELEPHONE LINE
- FIBER OPTIC LINE
- DRAIN TILE
- TREES
- CONSTRUCTION LIMITS
- CONSTRUCTION FENCE
- SITE FENCE
- SILT FENCE
- EXISTING TO BE DEMOLISHED
- CONCRETE WALK
- CURB AND GUTTER
- PROJECT BUILDING IDENTIFICATION
- BOLLARD
- CONSTRUCTION ENTRANCE AND CONSTRUCTION PAD PROTECTION, SIMILAR TO PRESTO GEOSYSTEMS GEOTERRA GTO OR EQUAL, HIGH DENSITY POLYETHYLENE INTERLOCKING MATS FOR EXISTING SURFACE PROTECTION, APPROXIMATELY 17.5" x 36.5" x 2" THICK INDIVIDUAL MATS CAPABLE OF BOLTING TO EACH OTHER TO FORM A CONTINUOUS PAD.
- TREE PROTECTION FENCE
- FLOW ARROW
- INLET PROTECTION
- WASH OUT AREA
- LANDSCAPING PLANT(ER) AREA
- TRAFFIC SIGN/CONTROL POLE

NOTE:
THIS IS A STANDARD LEGEND SHEET. THEREFORE SOME SYMBOLS OR ABBREVIATIONS MAY APPEAR ON THIS SHEET AND NOT ON THE PLANS.

 VETERANS AFFAIRS MEDICAL CENTER 500 E VETERANS ST TOMAH, WI 54660		CONSULTANTS:	PROJECT LEADER: DESIGN / BUILD SERVICES 1021 N. Superior, Unit 11 Tomah, Wisconsin 54660	Drawing Title CIVIL LEGEND AND GENERAL NOTES	Project Title Connect B406 AHU-5 to Emergency Power	FULLY SPRINKLERED 100% BD DOCUMENT	
				Approved: Project Director	Location Tomah, Wisconsin	Project Number 676-22-108	Office of Facilities Management
				Date November 20, 2025	Checked By: HFB	Drawn By: JMD	
				Revisions:	Date		

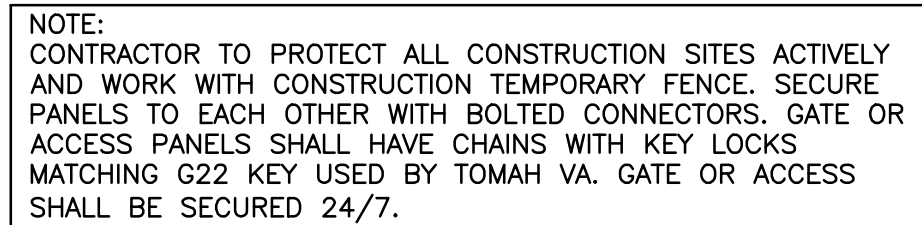

NORTH

A circular north arrow pointing upwards, with the word "NORTH" above it.

NORTH




1. REFER TO PHASING PLANS G1013, ALL WORK TO BE DONE IN ACCORDANCE WITH THE PHASES IDENTIFIED.
2. GENERAL CONTRACTOR TO REVIEW MECHANICAL, ELECTRICAL, AND ARCHITECTURAL PLANS FOR ADDITIONAL NEW WORK. ALL WORK FOR THE BUILDING SHALL BE COMPLETED PRIOR TO THE START OF THE FACILITY COMPLETE SYSTEM IS PART OF THE CONTRACTOR'S SCOPE OF WORK.
3. GENERAL CONTRACTOR IS RESPONSIBLE FOR THE COORDINATION OF ALL NEW CONSTRUCTION WORK.
4. MAINTAIN UTILITIES SERVICE TO ALL CAMPUS BUILDINGS AND ALL SPACES IN BUILDINGS. COORDINATE WITH VA COR FOR ANY DISRUPTION IN UTILITY SERVICES REQUIRED TO PERFORM WORK.
5. PLANS AND SECTIONS MAY NOT SHOW ALL REQUIRED PIPE, CONTRACTOR TO IDENTIFY AND LOCATE EXISTING UTILITY LINES, FANS, HVAC TERMINAL UNITS, CONTROL DEVICES AND VALVES. CONTRACTOR SHALL REFER TO MECHANICAL, ELECTRICAL, AND ARCHITECTURAL DRAWINGS FOR UTILITY LINES, DETAILS, AND DIAGRAMS FOR CONNECTIONS TO EQUIPMENT.
6. PROVIDE 3 WEEK WRITTEN NOTICE TO THE VA COR AND COR REPRESENTATIVES FOR ANY INTERRUPTION OF THE BUILDING UTILITIES, SYSTEMS OR RELATED SERVICES INCLUDING CONSTRUCTION RELATED ROAD CLOSURES OR CONFINED SPACE WORK.
7. CONTRACTOR SHALL ADHERE STRICTLY TO STATE AND FEDERAL OCCUPATIONAL SAFETY AND HEALTH ADMINISTRATION (OSHA) STANDARDS. A MINIMUM OF 10-HOUR OSHA TRAINING IS REQUIRED FOR ALL CONTRACT WORKERS ON SITE. TRAINING MUST BE CURRENT WITHIN THE LAST TWO YEARS.
8. CONTRACTOR SHALL PROVIDE WRITTEN CERTIFICATION THAT ALL CONTRACT WORKERS ON SITE HAVE BEEN SCREENED FOR TUBERCULOSIS WITHIN A MINIMUM OF 10-HOUR OSHA TRAINING TO THE WORK SITE AND HAVE BEEN FOUND TO HAVE NEGATIVE SCREENING REACTIONS.
9. ALL HOT WORK PERMITS MUST BE OBTAINED FROM THE VA FIRE DEPARTMENT. PERMIT IS VALID AS STATED ON FORM.
10. THE CONTRACTOR SHALL VERIFY ALL DIMENSIONS IN THE FIELD PRIOR TO STARTING CONSTRUCTION AND SHALL BE RESPONSIBLE FOR ALL FIELD DIMENSIONS. IF ANY DISCREPANCIES ARE FOUND TO EXIST, THE CONTRACTOR SHALL NOTIFY THE ENGINEER IMMEDIATELY.
11. THE GENERAL CONTRACTOR MAY CONTRACT WITH A PRIVATE UTILITY LOCATOR CONTRACTOR TO FIND AND LOCATE ALL BURIED UTILITIES. UNDERGROUND MAPPING PROVIDED IN THESE DOCUMENTS PERFORMED ON OCTOBER 31, 2025. LOCATIONS ARE NOT GUARANTEED. THIS CONTRACTOR SHALL USE THE SERVICES OF A CONTRACTOR SPECIALIZING IN DAYLIGHTING OR POT-HOLING TO VERIFY UNDERGROUND UTILITIES BEFORE EXCAVATION OR DIRECTIONAL BORING TAKES PLACE.
12. ALL RESTORATION FOR LAWN, SIDEWALK, ROADWAYS, AND ALL EXTERIOR FEATURES SHALL BE COMPLETED WITHIN 15 WORKING DAYS AFTER THE COMPLETION OF THE END OF SITE TRAINING TASK OF WORK, UNLESS OTHERWISE DESCRIBED OR NOTED IN THESE DOCUMENTS. COOPERATE AND OTHERWISE WORK WITH THE VA COR TO REPAIR AND RESTORE ALL EXISTING TRENCHES, AND QUICKLY COMPLETE CONTRACTORS DUTIES.

- ① CONSTRUCTION FENCE, SEE DETAIL 1 ON C501.
- ② PROVIDE THE REQUIRED 6' WIDE FENCE OPENING WITH 2 PERSONNEL ACCESS GATES, NOT SHOWN, COORDINATE LOCATION WITH SAFETY REQUIREMENTS.
- ③ SILT FENCE, SEE DETAIL 7 ON DWG C501.
- ④ CONSTRUCTION SITE SIGN, SEE DETAIL 2 ON DWG C501.
- ⑤ CONSTRUCTION FENCE WARNING SIGN, SEE DETAIL 5 ON DWG C501.
- ⑥ CONSTRUCTION SAFETY SIGN, SEE DETAIL 8 ON DWG C501.
- ⑦ REMOVE EXISTING CONCRETE STOOP COMPLETE.
- ⑧ PROVIDE CONSTRUCTION TRUCK PAD AND EROSION CONTROL. SEE DETAILS 4 AND 6 ON C501.
- ⑨ EXCAVATE FOR NEW DUCTBANK. THE CONTRACTOR IS REQUIRED TO HIRE THE SERVICES OF A POTHOLE/ DAYLIGHT CONTRACTOR TO VERIFY LOCATIONS SHOWN ON THE UNDERGROUND MAPPING PLAN BEFORE EXCAVATION BEGINS.
- ⑩ ELECTRICAL CONTRACTOR SHALL REMOVE THE EXISTING CONDUCTORS AFTER THE EXISTING CHILLER IS CONNECTED TO ITS NEW CONDUCTORS. ELECTRICAL CONTRACTOR TO PROVIDE A WATERPLUG PLUG INSIDE B406 UTILITY TUNNEL AT THE EXISTING PULL BOX. BURIED CONDUIT IS NOW AN EMPTY SPARE.
- ⑪ PROVIDE TRENCH BOX. OPTIONAL: PROVIDE SHORING FOR EXCAVATION WORK.
- ⑫ SEE NOTES FOR REQUIRED DEWATERING AT ALL EXCAVATION WORK.
- ⑬ EX. BURIED CONDUIT WITH POWER FOR CHILLER, SEE ELECTRICAL DRAWINGS FOR REQUIREMENTS.
- ⑭ CONTRACTOR TO HAND DIG TO EXPOSE CONDUIT, DUCTBANK, AND EXISTING BURIED UTILITIES HERE.

 Department of
Veterans Affairs



PCG
DESIGN / BUILD SERVICES
1021 N. Superior, Unit 11
Tomah, Wisconsin 54660

CD101

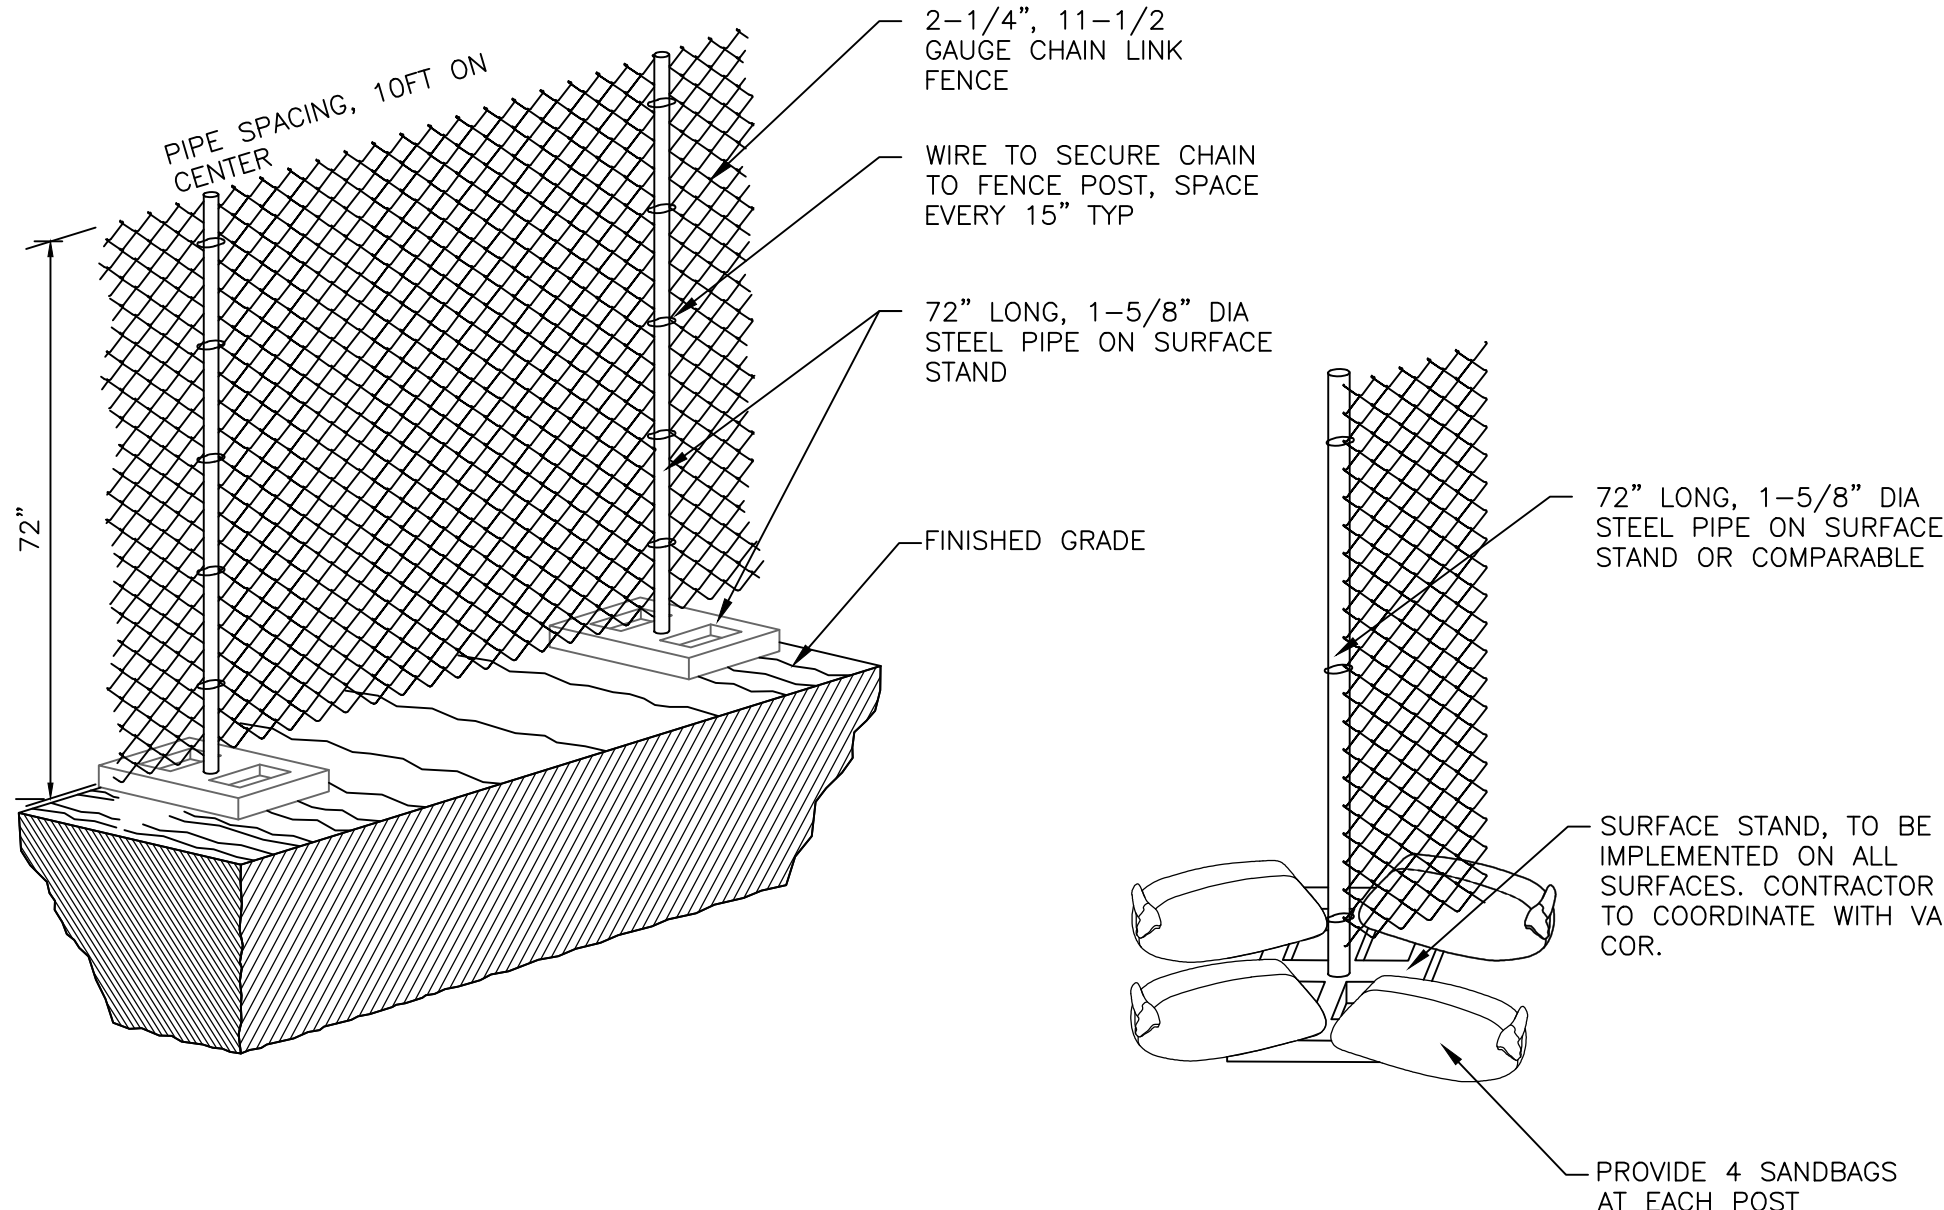

- NOTE:
- CHAIN LINK CONSTRUCTION FENCING IS TO BE INSTALLED PRIOR TO COMMENCING CONSTRUCTION ACTIVITIES.
 - CHAIN LINK CONSTRUCTION FENCE SHALL BE A MINIMUM OF 72" ABOVE GRADE.
 - FENCE SHALL BE INSPECTED DAILY AFTER CONSTRUCTION ACTIVITIES HAVE BEEN COMPLETED FOR THE DAY. IF DAMAGED, FENCING SHALL BE REPAIRED IMMEDIATELY.
 - CHAIN LINK CONSTRUCTION FENCE IS SHOWN ON IMPERVIOUS SURFACES, SUCH AS THE EXISTING DRIVE AND PARKING AND GRASS AREAS. POST ARE TO BE ANCHORED ON SURFACE STANDS. STEEL PIPE IS NOT TO BE DRIVEN BELOW GRADE.



1 TEMPORARY CHAIN LINK FENCE DETAIL
SCALE: NTS

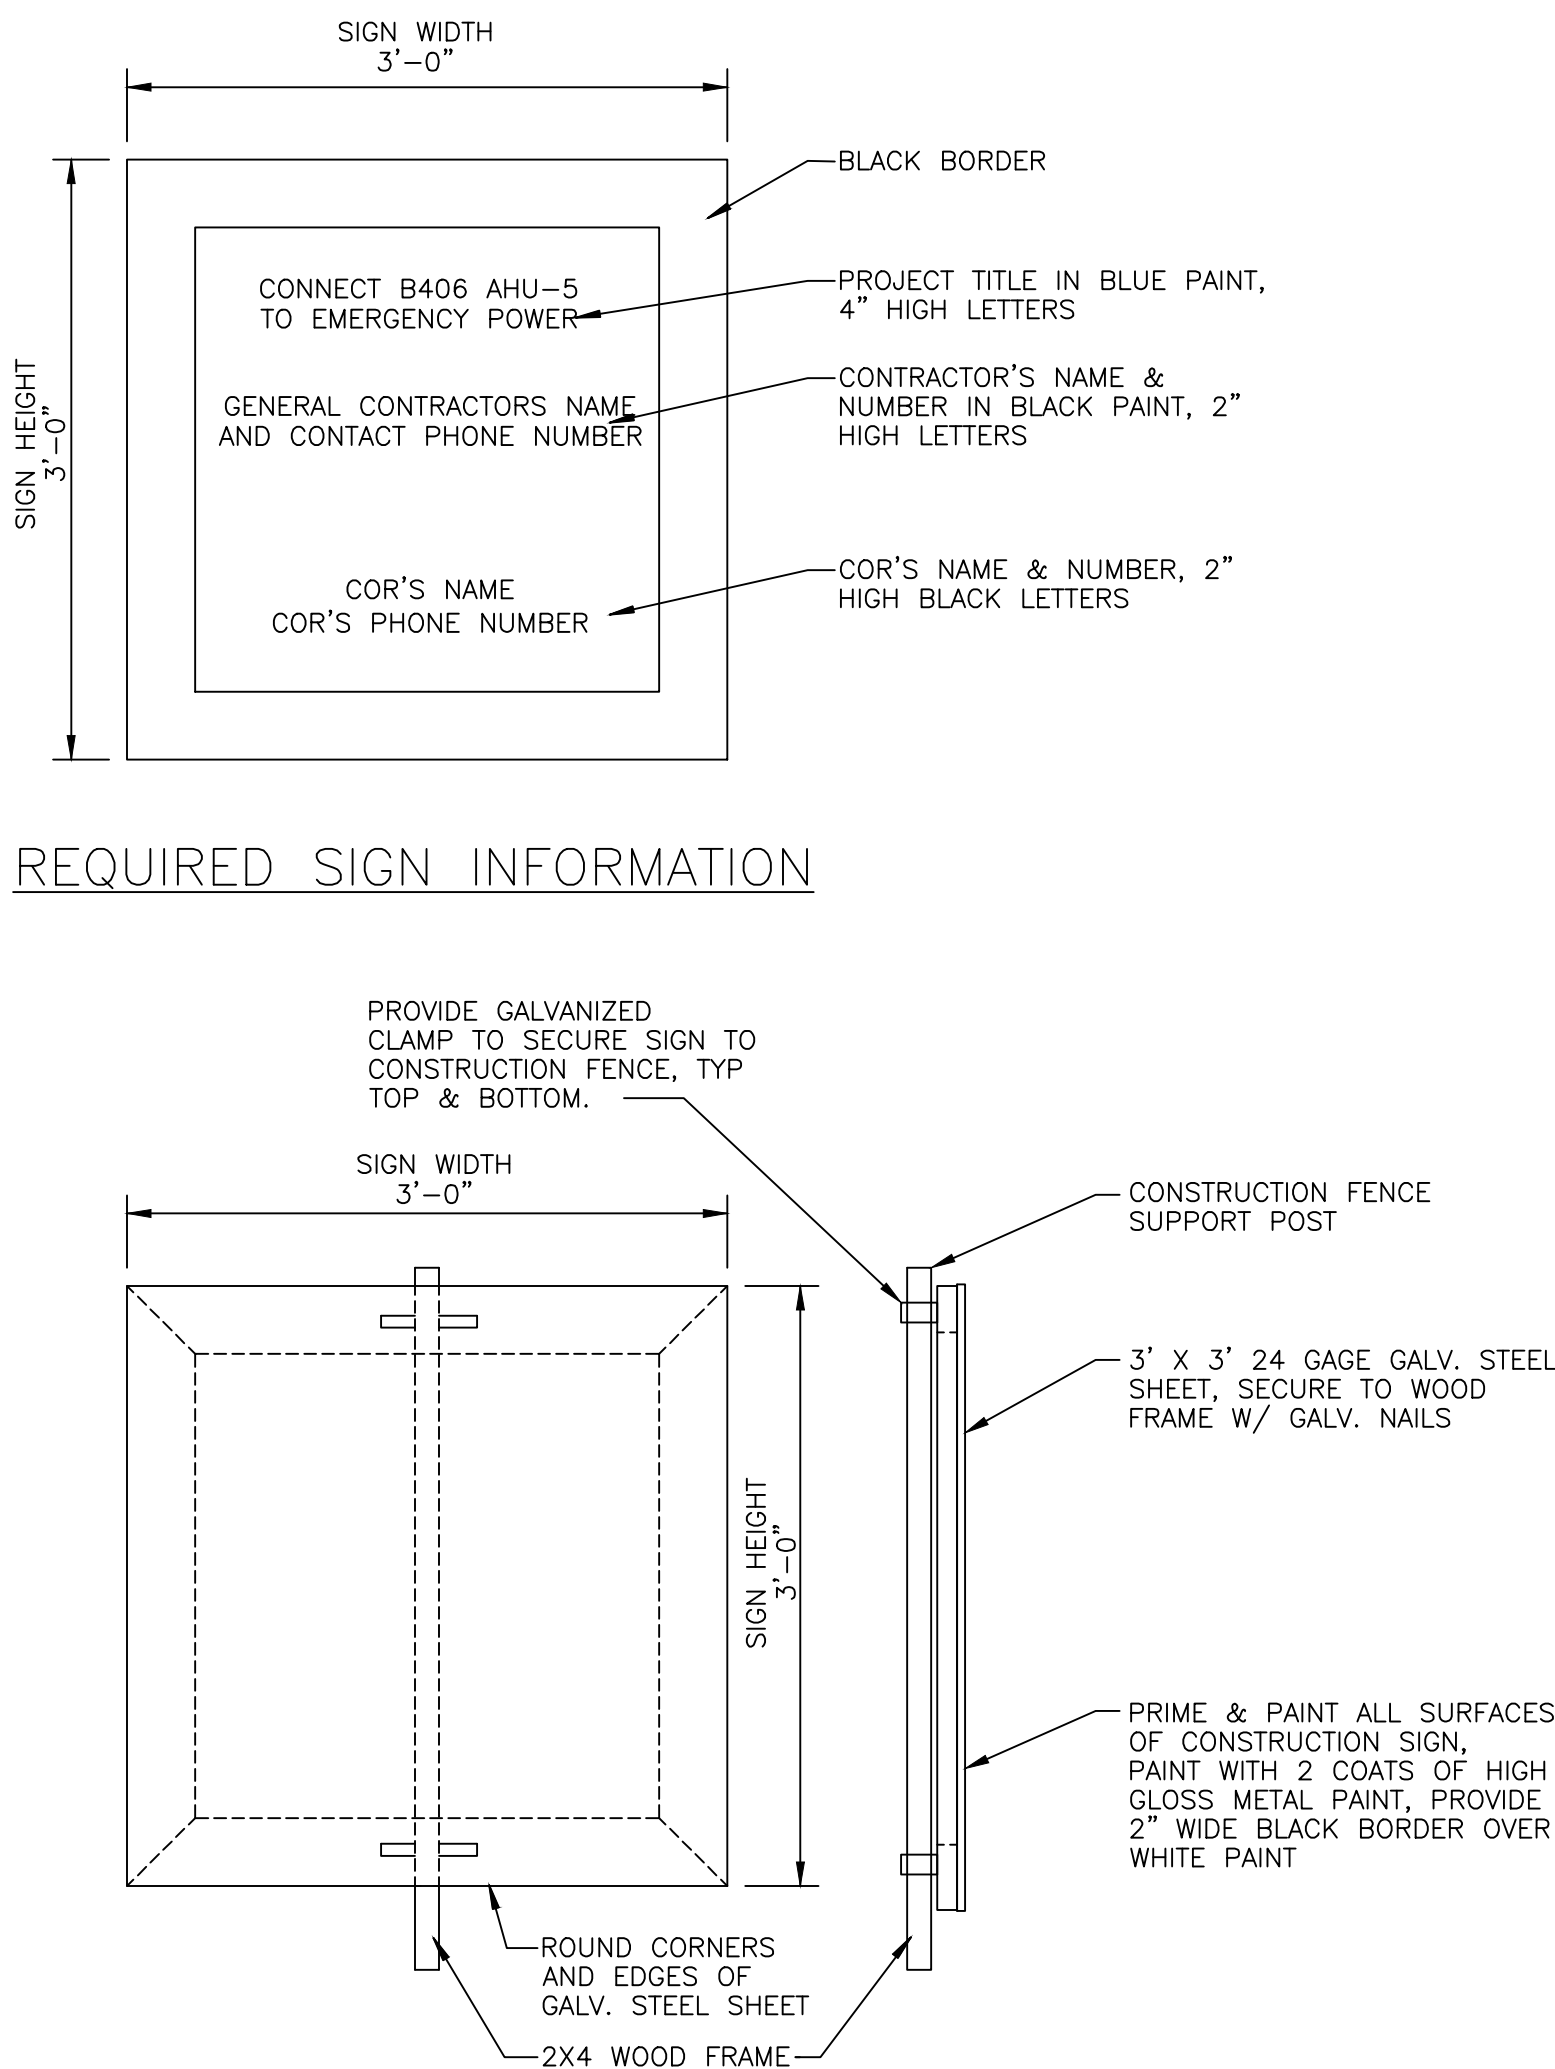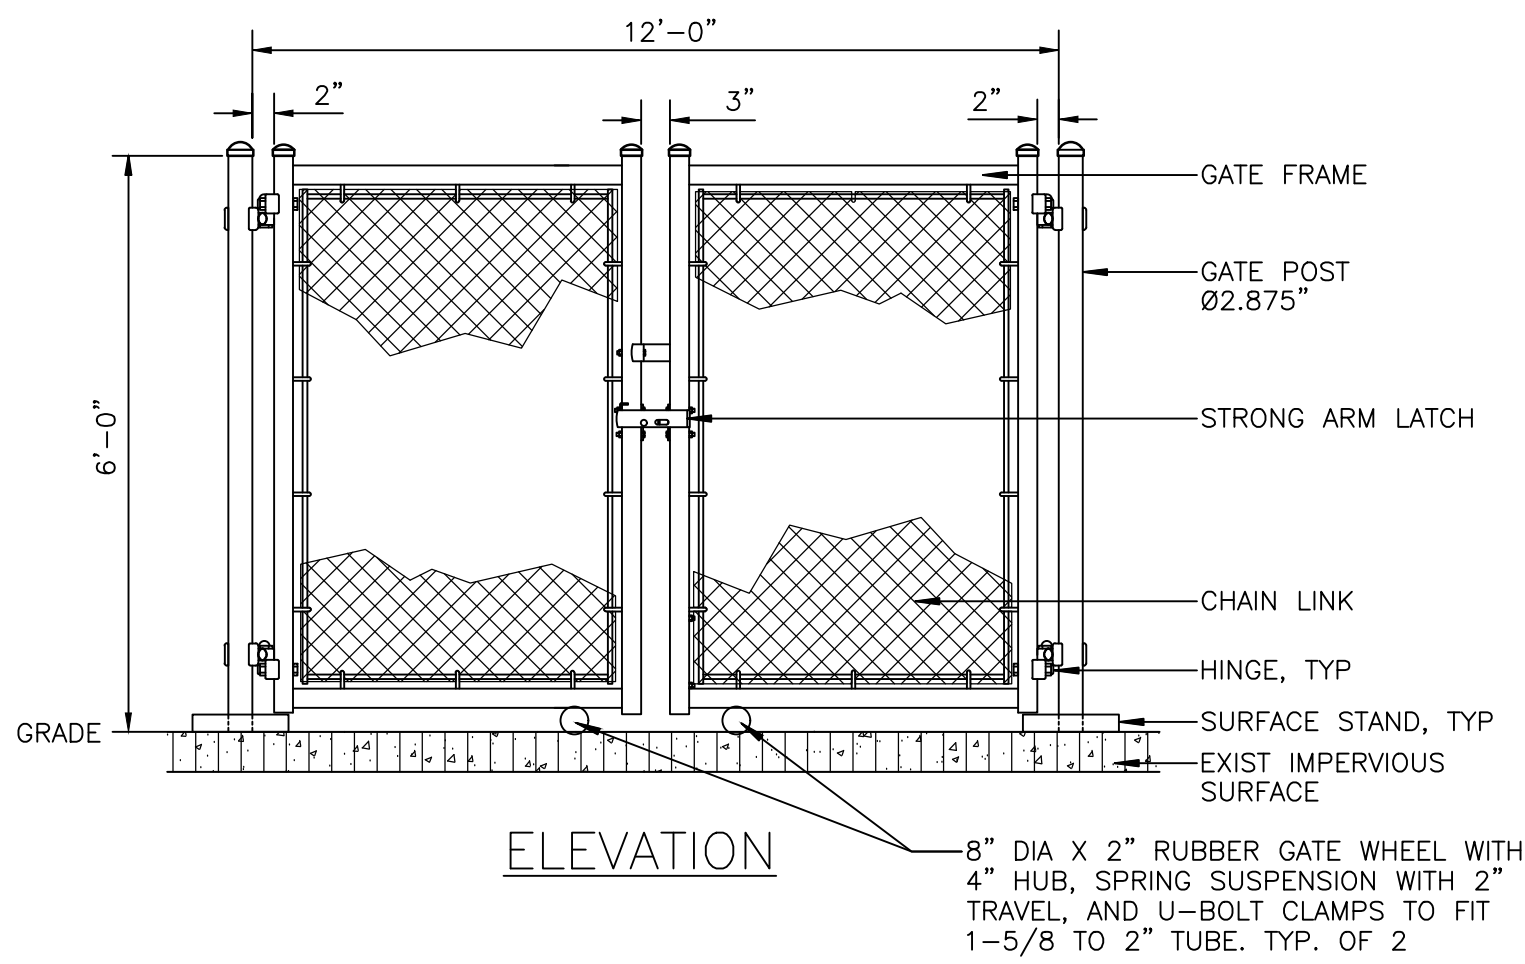


3 STOOP DETAIL
SCALE: NOT TO SCALE

SIGN CONSTRUCTION & MOUNTING
NOTE:
SEE 1.29 OF SECTION 01 00 00 GENERAL REQUIREMENTS


2 CONSTRUCTION SIGN DETAIL
SCALE: NTS

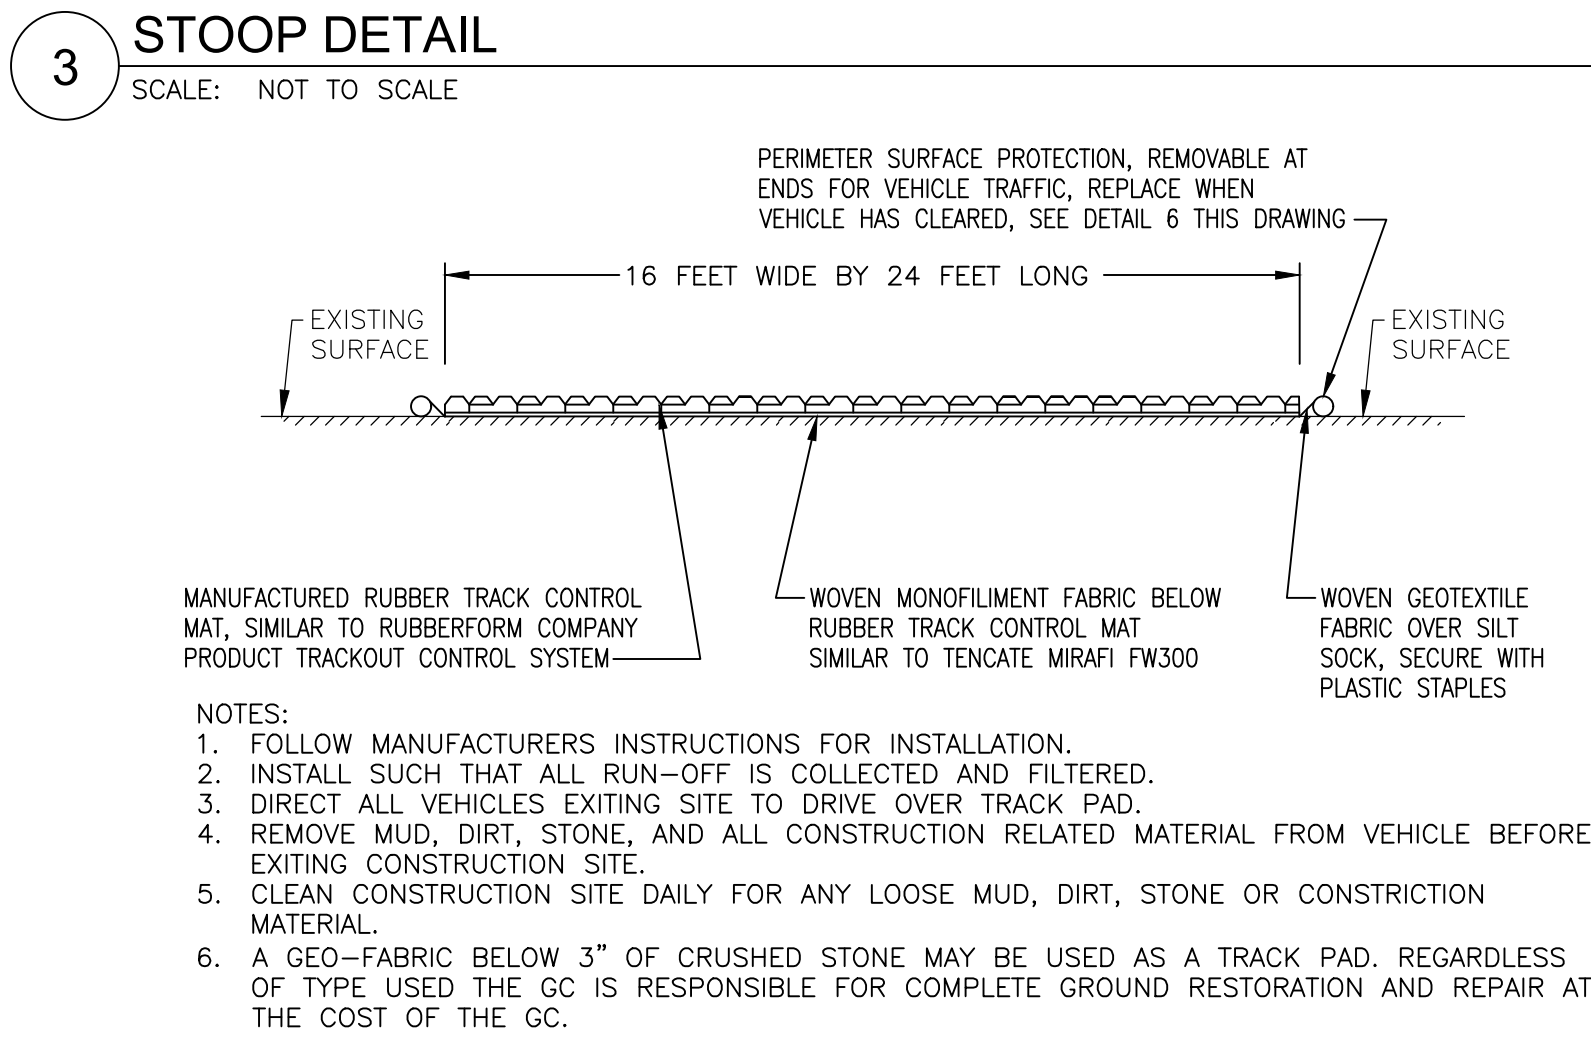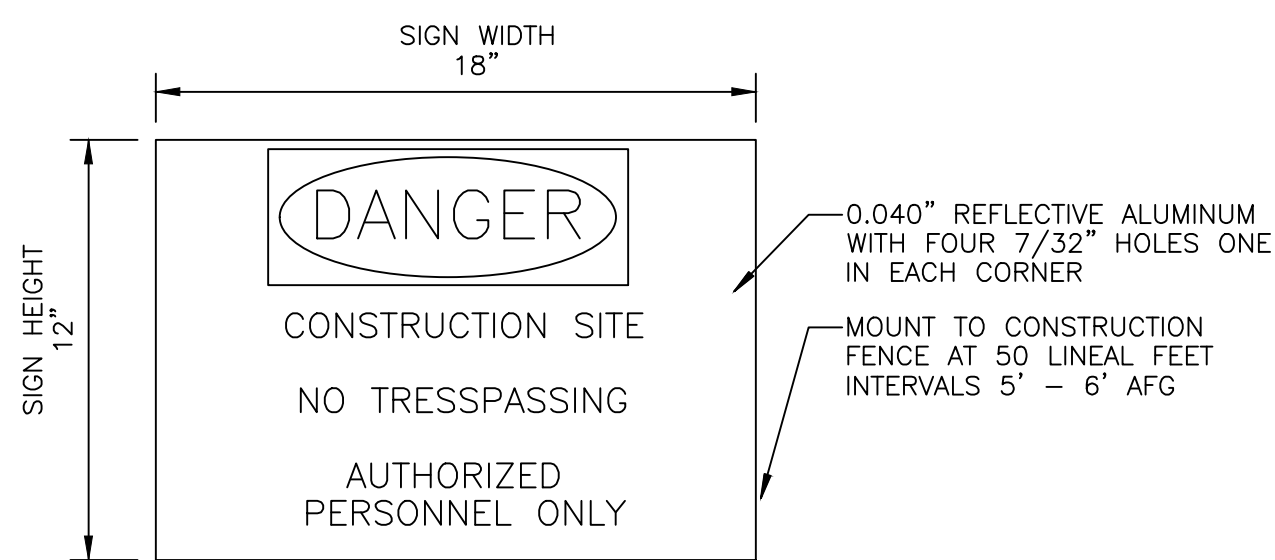

4 CONSTRUCTION TRACK PAD DETAIL
SCALE: NTS

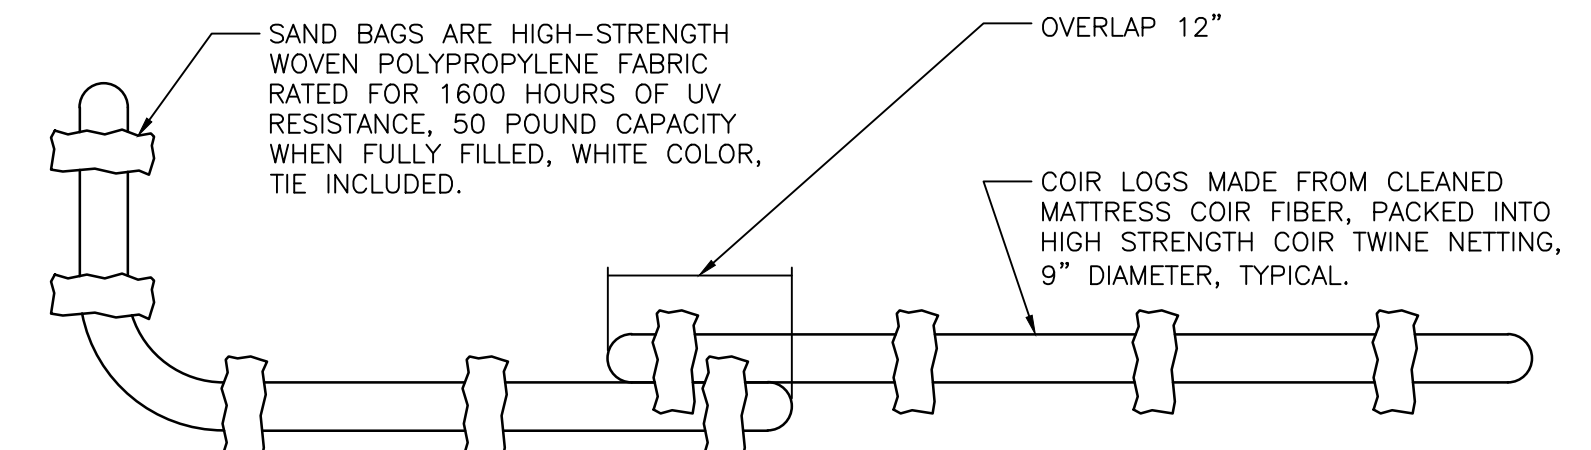


6 PERIMETER SURFACE EROSION CONTROL DETAIL
SCALE: NOT TO SCALE

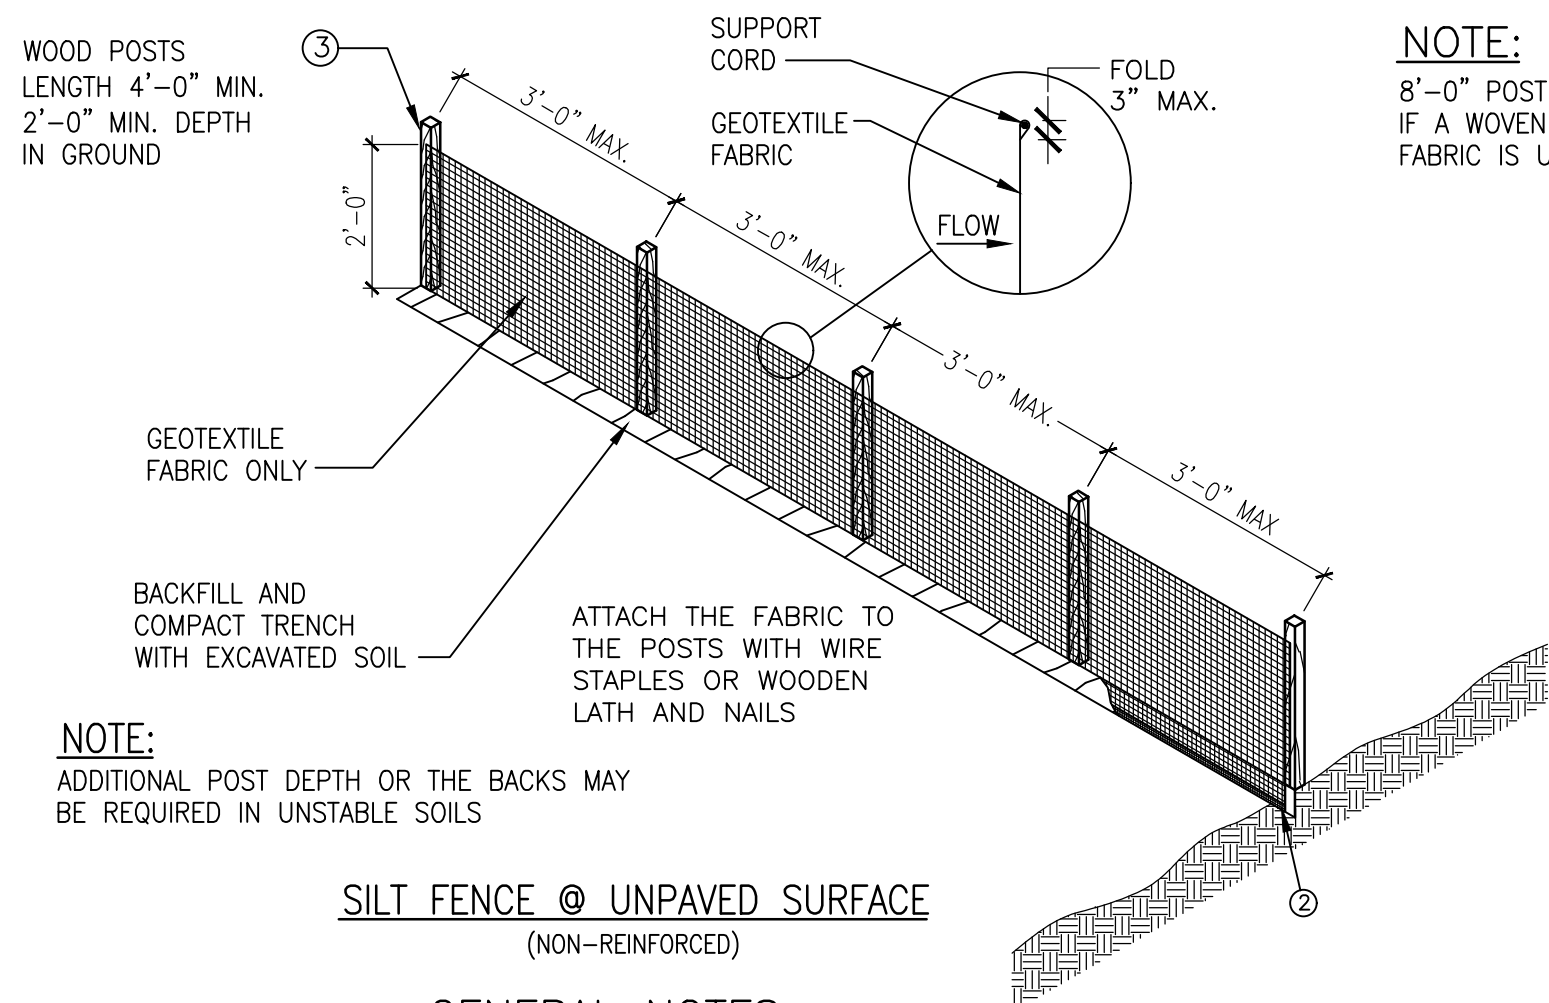


- GENERAL NOTES:
- DETAILS OF CONSTRUCTION NOT SHOWN ON THIS DRAWING SHALL CONFORM TO THE PERTINENT REQUIREMENTS OF THE STANDARD SPECIFICATIONS AND APPLICABLE SPECIAL PROVISIONS.
- HORIZONTAL BRACE WITH 2" x 4" WOODEN FRAME OR EQUIVALENT AT TOP OF POSTS AS DIRECTED BY THE ENGINEER.
 - TRENCH SHALL BE A MINIMUM OF 4" WIDE AND 6" DEEP TO BURY AND ANCHOR THE GEOTEXTILE FABRIC. FOLD MATERIAL TO FIT TRENCH AND BACKFILL AND COMPACT TRENCH WITH EXCAVATED SOIL.
 - WOOD POST SHALL BE A MINIMUM SIZE OF 1 1/8" x 1 1/8" OF OAK OR HICKORY

7 TEMPORARY SILT FENCE DETAIL
SCALE: NTS

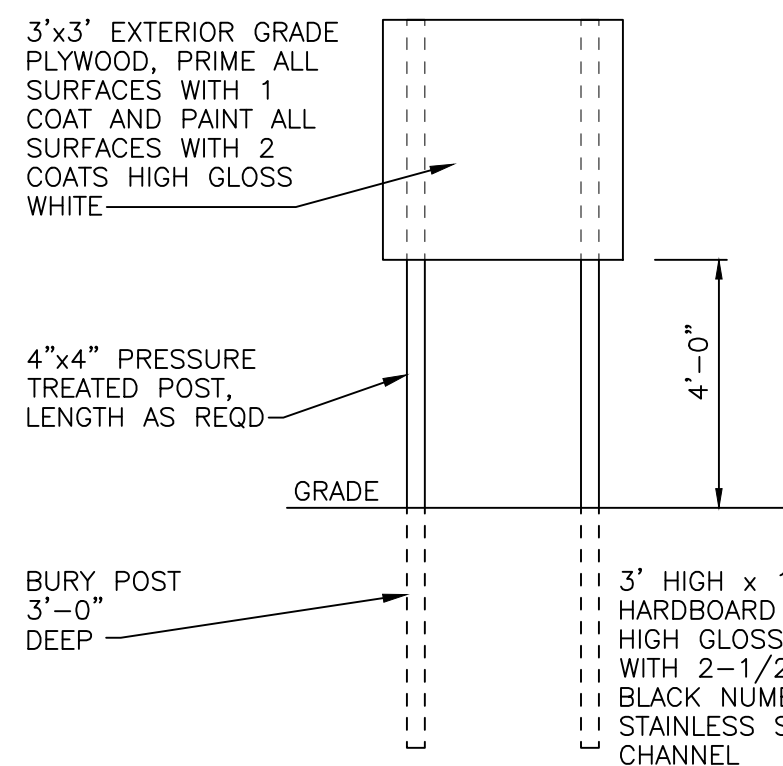

8 SAFETY SIGN DETAIL
SCALE: NTS

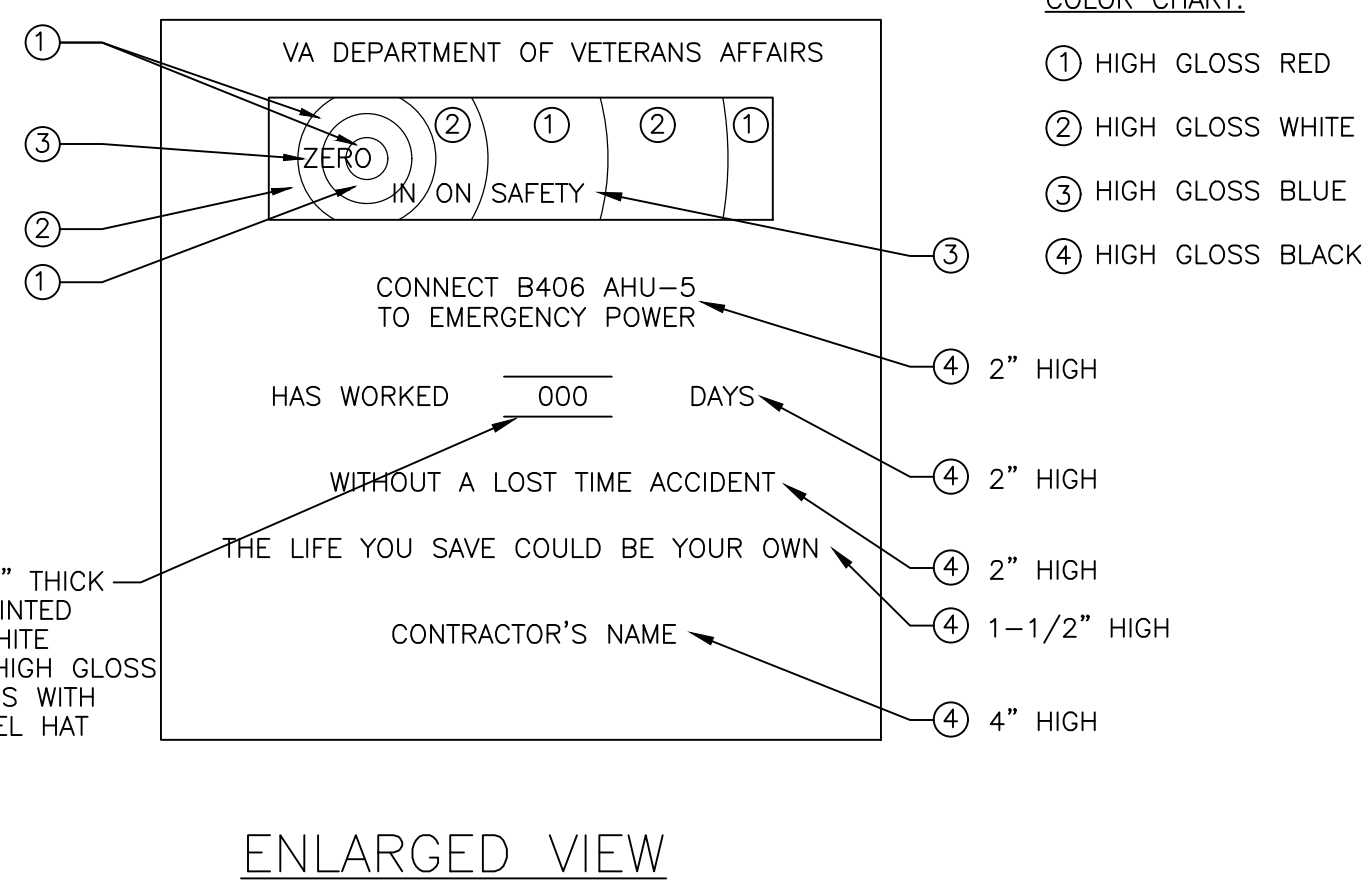

Revisions:	Date



VETERANS AFFAIRS
MEDICAL CENTER
500 E VETERANS ST
TOMAH, WI 54660



CONSULTANTS:

PROJECT LEADER:



Drawing Title
CIVIL
DETAILS

Approved: Project Director

Project Title
Connect B406 AHU-5 to
Emergency Power

Location
Tomah, Wisconsin

Date
November 20, 2025

Checked By:
HFB

Drawn By:
JMD


FULLY SPRINKLERED
100% BD DOCUMENT

Project Number
676-22-108
Building Number

Drawing Number
C501

Office of
Facilities
Management



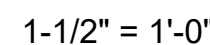

0'-0" CEILING HEIGHT

 Department of
Veterans Affairs

three inches = one foot
one and one half inches = one foot
one inch = one foot
three quarters inch = one foot
one half inch = one foot
three eighths inch = one foot
one quarter inch = one foot
one eighth inch = one foot




GENERAL NOTES

1. REFER TO GC SHEETS FOR IC/PHASING PLANS. ALL WORK TO BE DONE IN ACCORDANCE WITH THE PHASES IDENTIFIED.
2. GENERAL CONTRACTOR SHALL REVIEW MECHANICAL, ELECTRICAL, PLUMBING AND FIRE PROTECTION PLANS FOR ADDITIONAL CONSTRUCTION WORK.
3. GENERAL CONTRACTOR IS RESPONSIBLE FOR THE COORDINATION OF ALL CONSTRUCTION WORK.
4. MAINTAIN CONTINUOUS UTILITY SERVICE TO ALL SPACES IN THE BUILDING NOT AFFECTED BY THIS WORK. COORDINATE WITH VA COR ANY DISRUPTION IN SERVICES REQUIRED TO PERFORM WORK.
5. PATCH ALL SURFACES DISTURBED BY DEMOLITION TO CREATE A SMOOTH AND CONSISTENT FINISH WITH ADJACENT MATERIALS. TYPICAL AT FLOORS, WALLS, AND CEILINGS.
6. DIMENSIONS ON FLOOR PLAN ARE BASED ON FACE OF FINISHED WALL TO FACE OF FINISHED WALL (NOMINAL).

KEYED NOTES

- ① NEW 6" CONCRETE EQUIPMENT PAD, SEE DETAIL 1 ON SHEET A001. COORDINATE SIZE AND LOCATION WITH MECHANICAL CONTRACTOR.
- ② LOCATION OF NEW ELECTRICAL CONDUIT THROUGH EXISTING WALL. CORE HOLE, SEAL NEW PENETRATIONS. SEE ELECTRICAL DRAWINGS FOR REQUIREMENTS.
- ③ LOCATION OF NEW REFRIGERANT PIPES THROUGH EXISTING WALL. CORE HOLE, SEAL NEW PENETRATIONS. SEE MECHANICAL AND ELECTRICAL DRAWINGS FOR REQUIREMENTS.
- ④ WALL PATCHING WITH GROUT AND PAINTING REQUIRED. SEE DRAWING EP103 FOR REQUIRED WORK.
- ⑤ DEMOLISH EXISTING STOOP, PROVIDE NEW STOOP, SEE CIVIL DRAWINGS FOR REQUIREMENTS.
- ⑥ CORE HOLE IN EXISTING B406 UTILITY TUNNEL. SEAL PENETRATIONS. SEE ELECTRICAL DRAWINGS FOR REQUIREMENTS.
- ⑦ COORDINATE ALL CORING WITH HAZARDOUS PLAN HA101 AND HAZARDOUS CONTRACTOR.


1 FIRST FLOOR PLAN
1/4"= 1'-0"

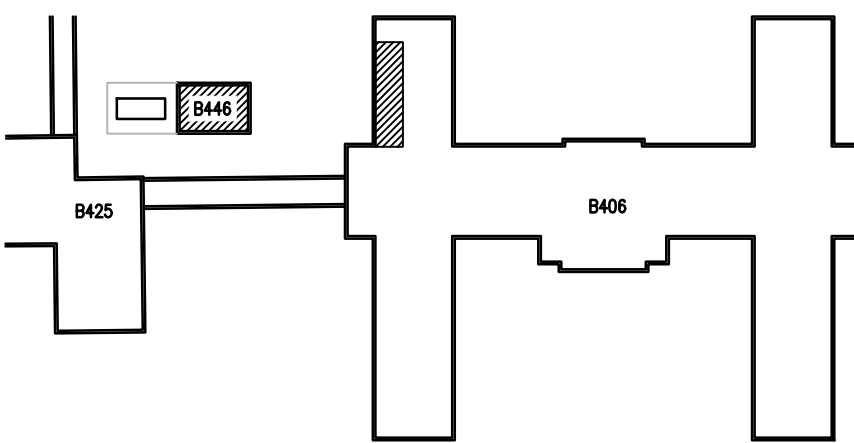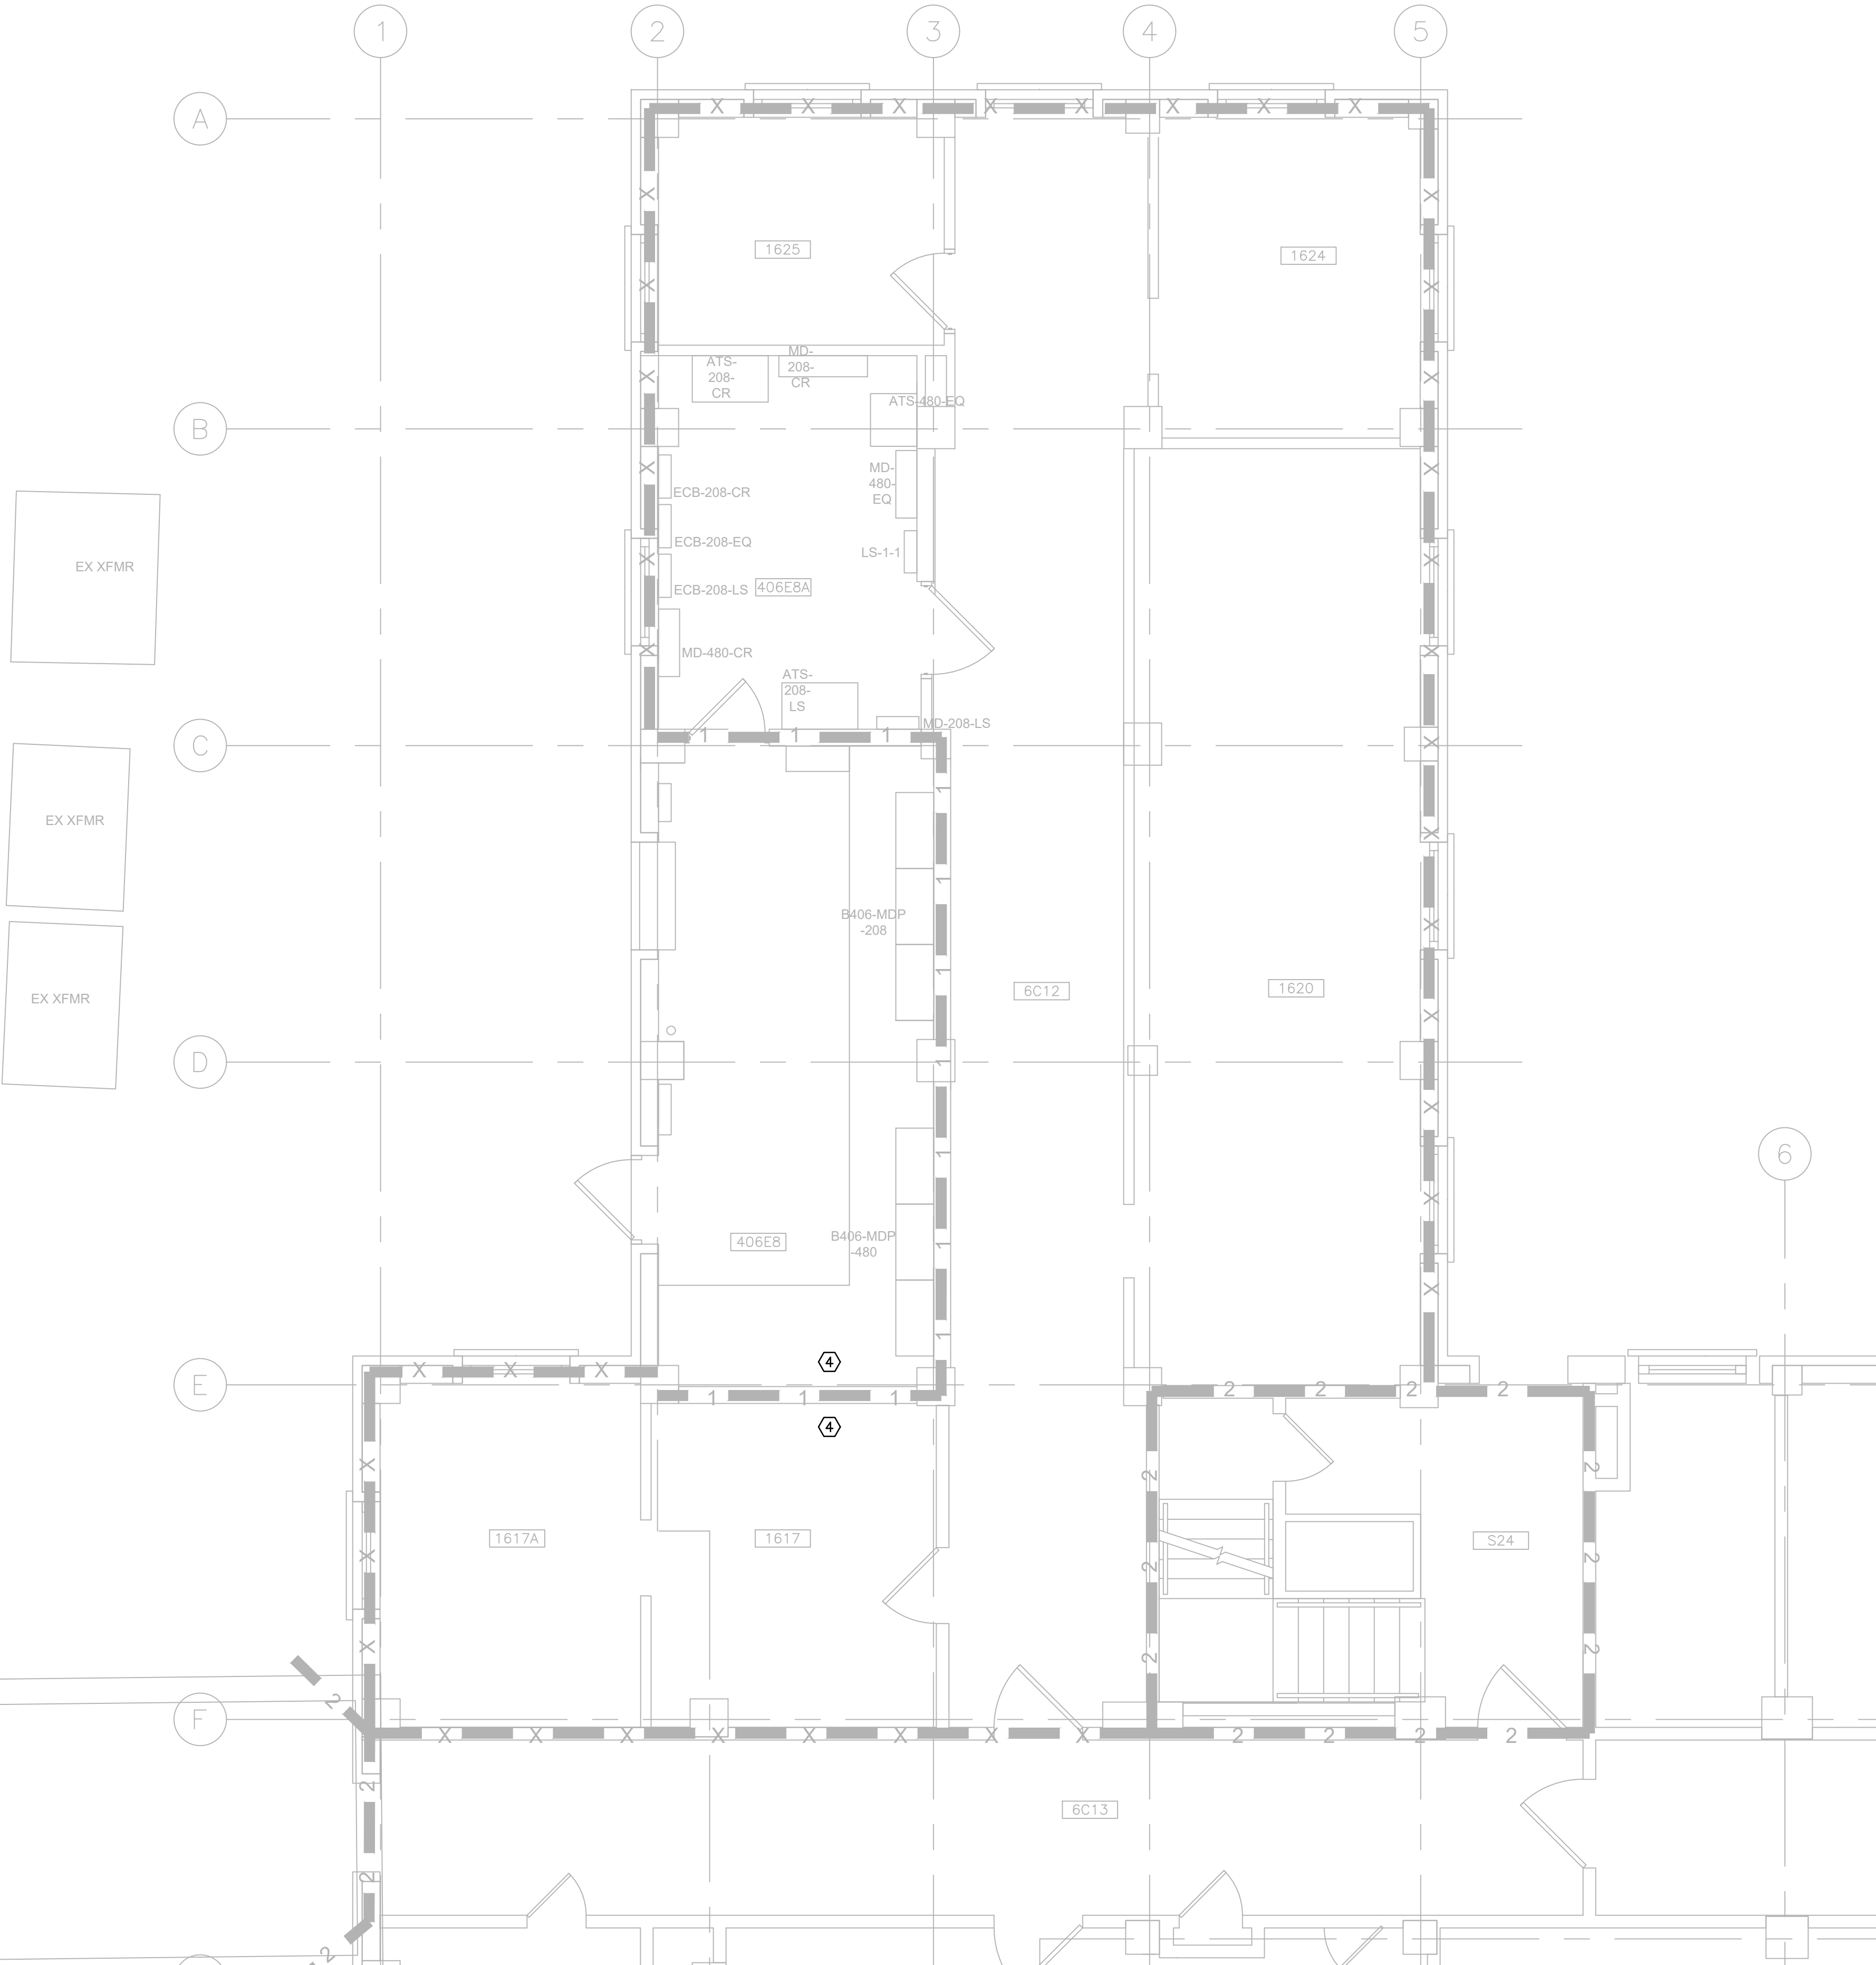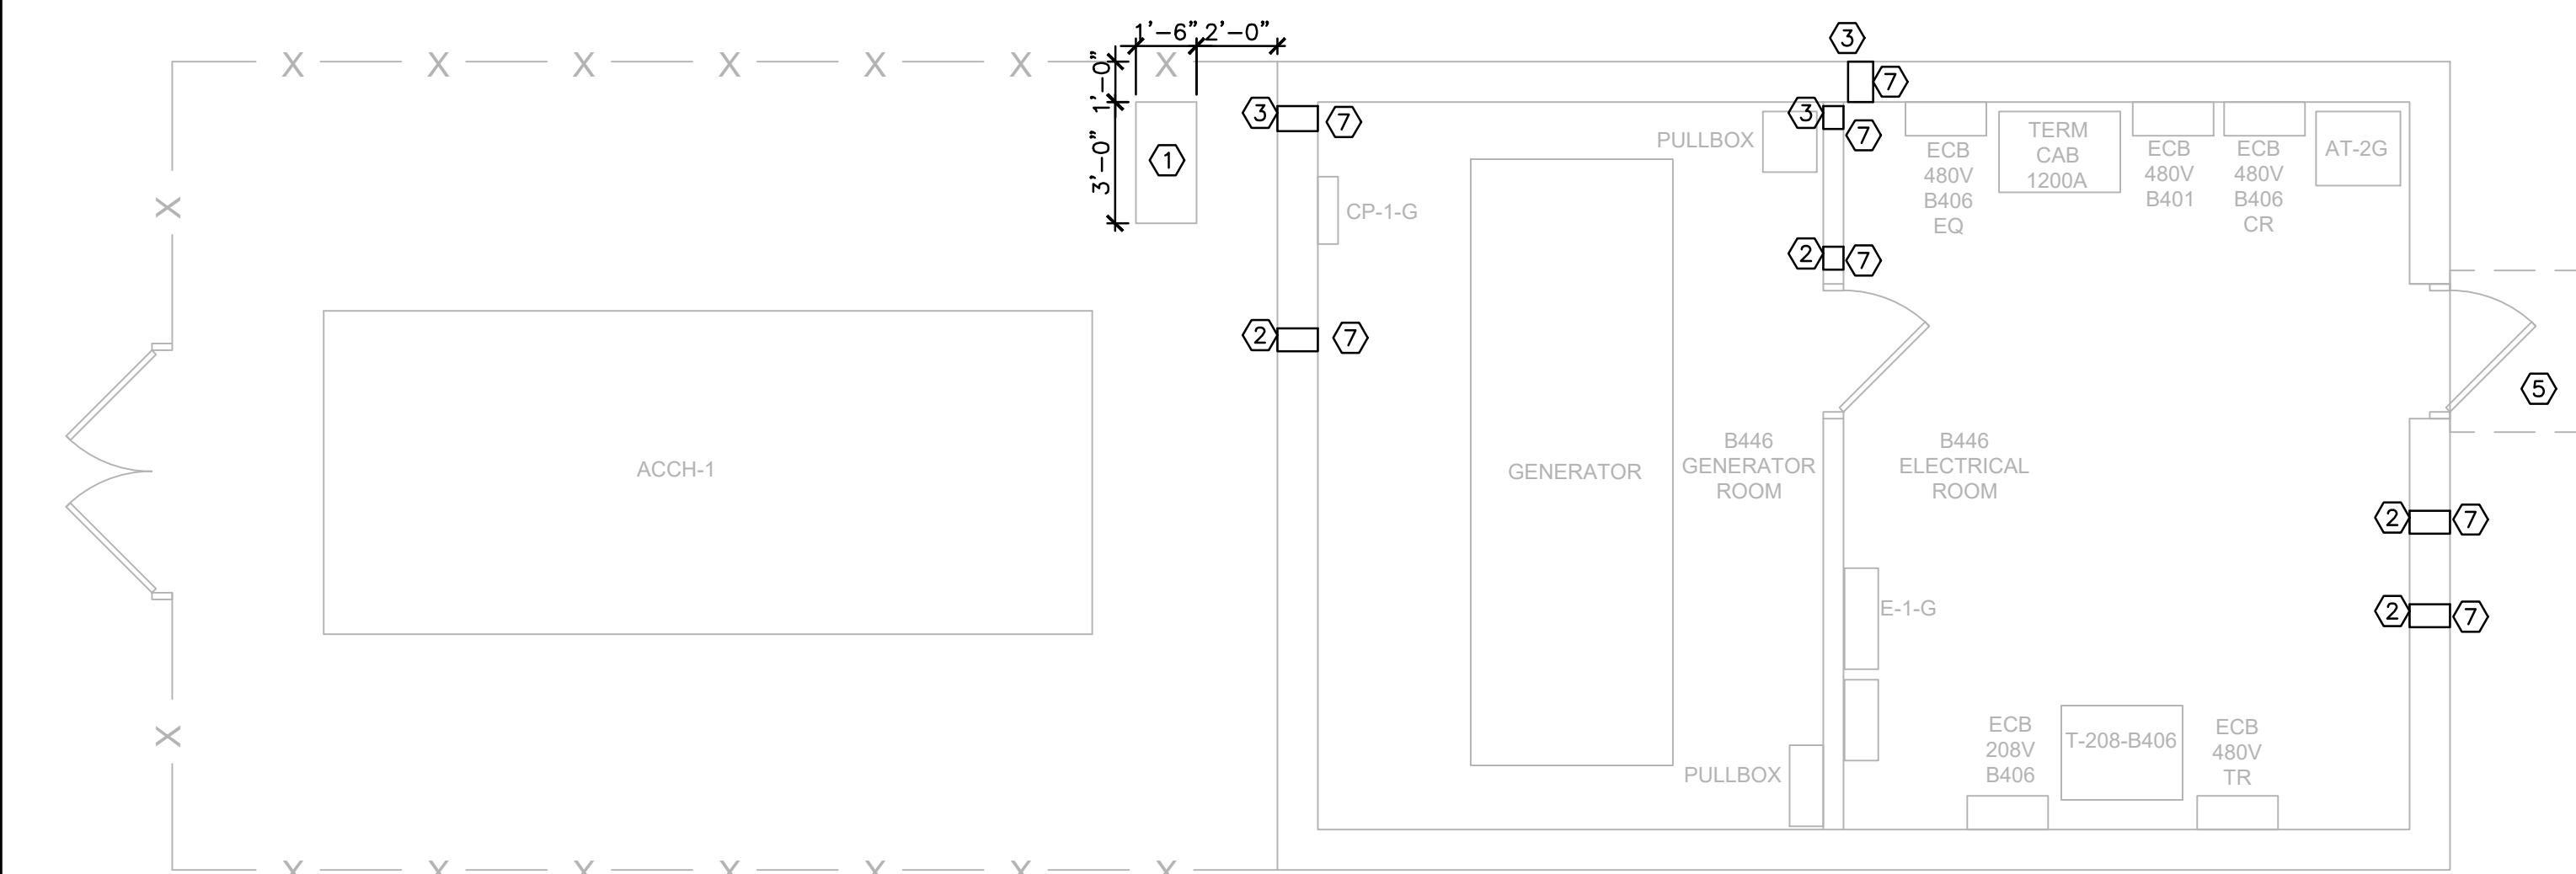

KEY PLAN
NORTH
FULLY SPRINKLERED
100% BD DOCUMENT


	</
--	--	----

three inches = one foot
one and one half inches = one foot
one inch = one foot
three quarters inch = one foot
one half inch = one foot
three eighths inch = one foot
one quarter inch = one foot
one eighth inch = one foot

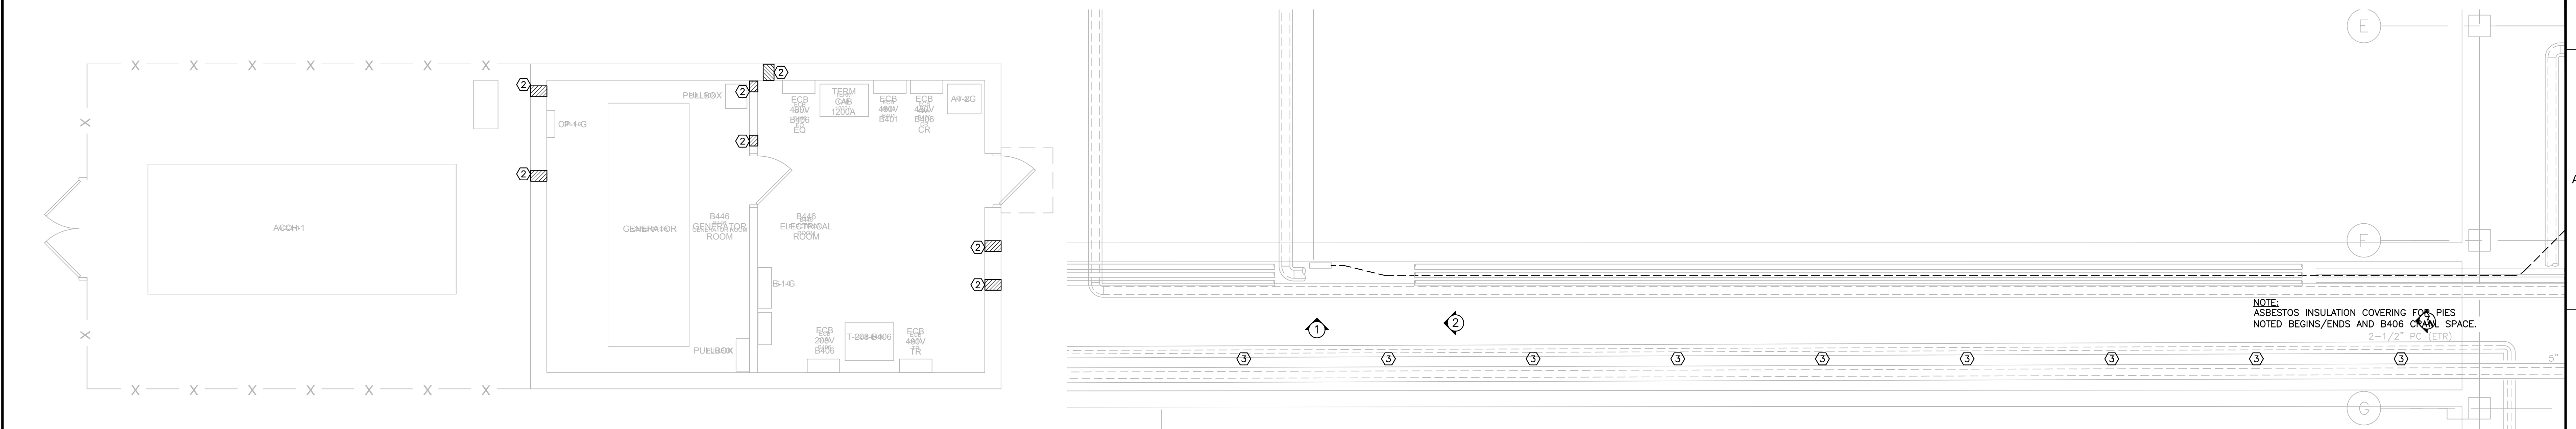


1 FIRST FLOOR PLAN - B446
1/4"= 1'-0"

3 TRAMWAY TUNNEL B406
1/4"= 1'-0"

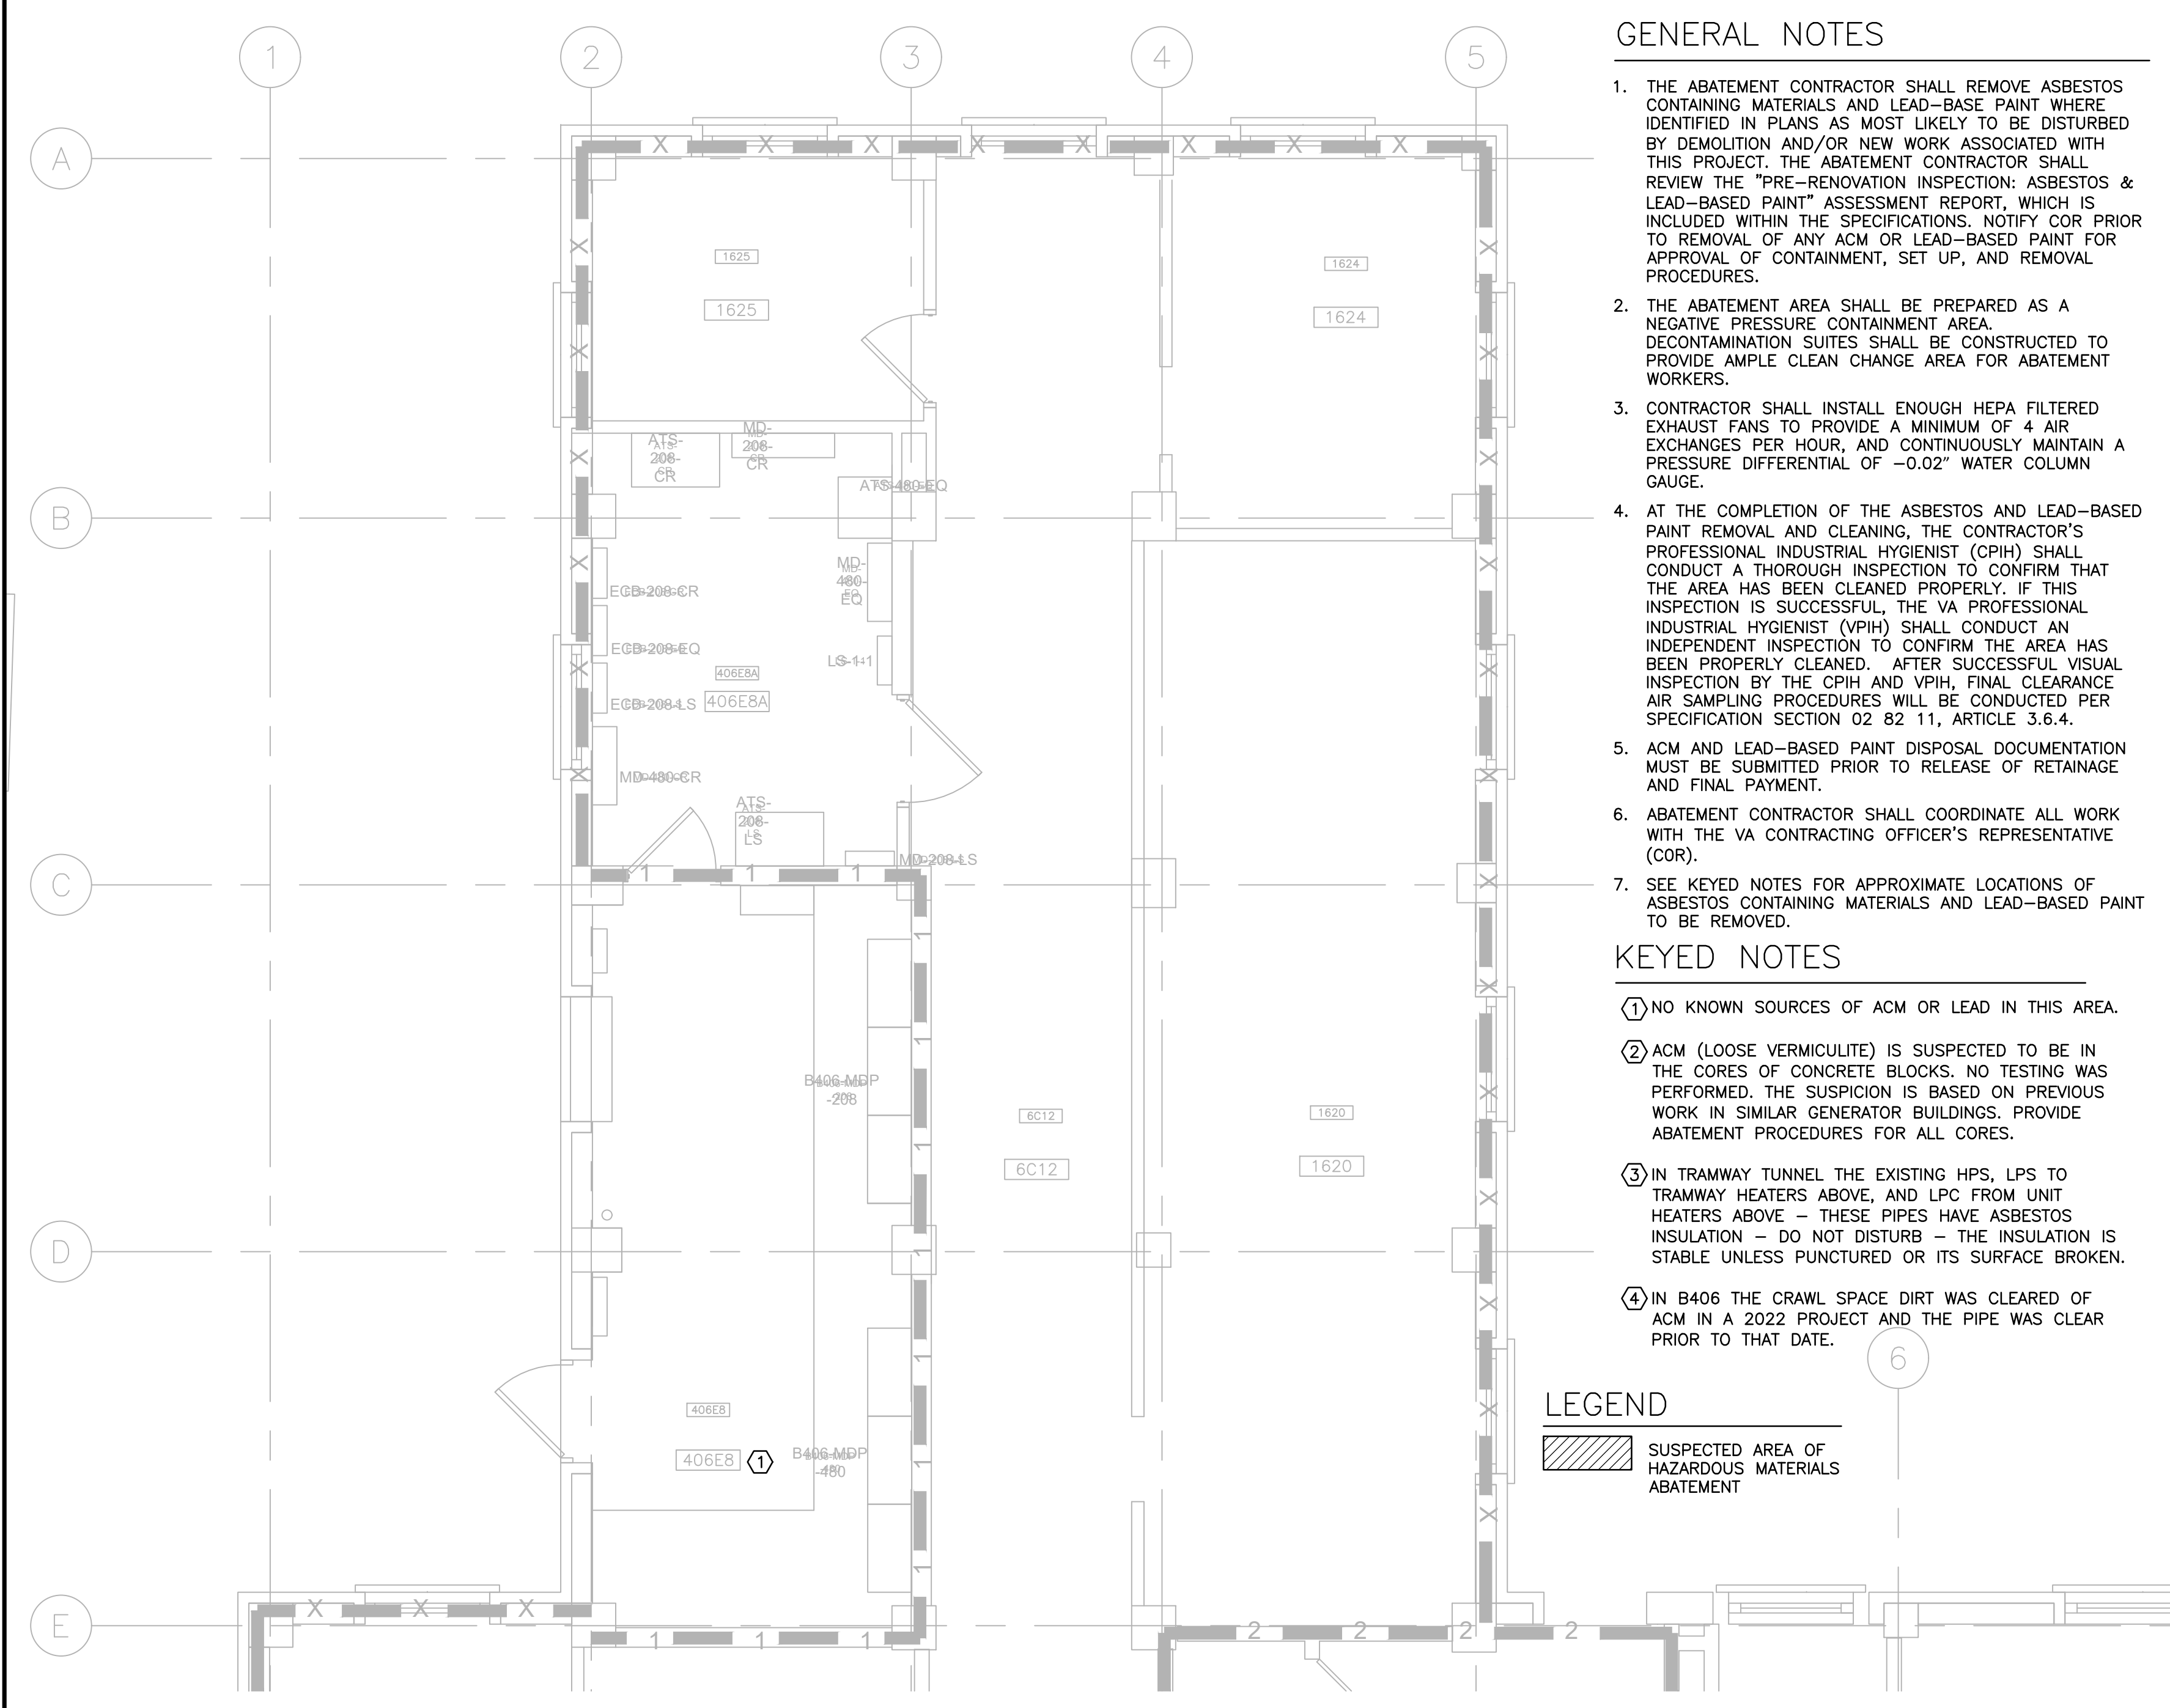

2 PARTIAL FIRST FLOOR PLAN - B406
1/4"= 1'-0"

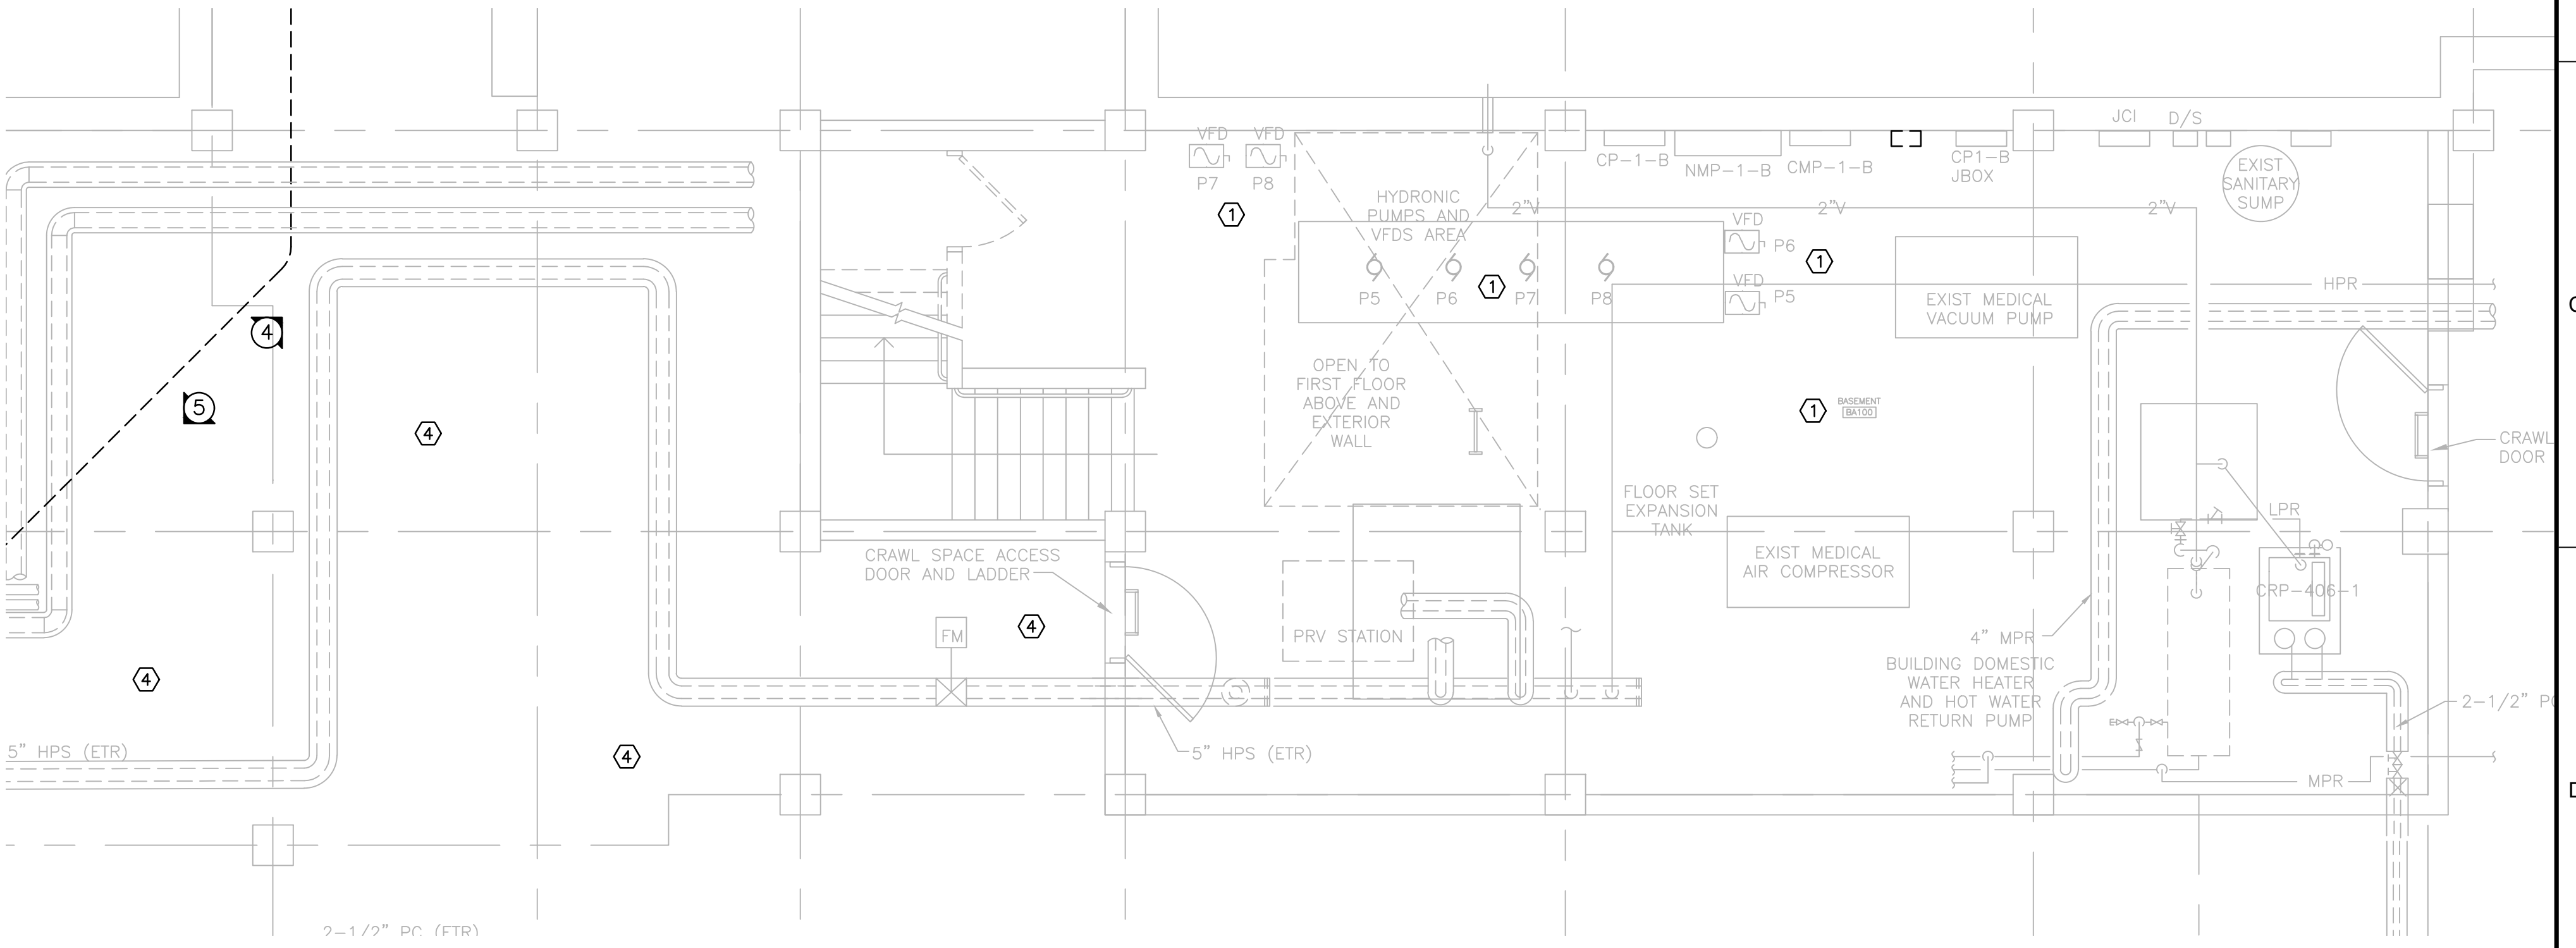

4 CRAWL SPACE AND MECHANICAL ROOM B406
1/4"= 1'-0"

GENERAL NOTES


1. THE ABATEMENT CONTRACTOR SHALL REMOVE ASBESTOS CONTAINING MATERIALS AND LEAD-BASED PAINT WHERE IDENTIFIED IN PLANS AS MOST LIKELY TO BE DISTURBED BY DEMOLITION AND/OR NEW WORK ASSOCIATED WITH THIS PROJECT. THE ABATEMENT CONTRACTOR SHALL REVIEW THE "PRE-RENOVATION INSPECTION: ASBESTOS & LEAD-BASED PAINT" ASSESSMENT REPORT, WHICH IS INCLUDED WITHIN THE SPECIFICATIONS. NOTIFY COR PRIOR TO REMOVAL OF ANY ACM OR LEAD-BASED PAINT FOR APPROVAL OF CONTAINMENT, SET UP, AND REMOVAL PROCEDURES.
2. THE ABATEMENT AREA SHALL BE PREPARED AS A NEGATIVE PRESSURE CONTAINMENT AREA. DECONTAMINATION SUITES SHALL BE CONSTRUCTED TO PROVIDE AMPLE CLEAN CHANGE AREA FOR ABATEMENT WORKERS.
3. CONTRACTOR SHALL INSTALL ENOUGH HEPA FILTERED EXHAUST FANS TO PROVIDE A MINIMUM OF 4 AIR EXCHANGES PER HOUR, AND CONTINUOUSLY MAINTAIN A PRESSURE DIFFERENTIAL OF -0.02" WATER COLUMN GAUGE.
4. AT THE COMPLETION OF THE ASBESTOS AND LEAD-BASED PAINT REMOVAL AND CLEANING, THE CONTRACTOR'S PROFESSIONAL INDUSTRIAL HYGIENIST (CPIH) SHALL CONDUCT A THOROUGH INSPECTION TO CONFIRM THAT THE AREA HAS BEEN CLEANED PROPERLY. IF THIS INSPECTION IS SUCCESSFUL, THE VA PROFESSIONAL INDUSTRIAL HYGIENIST (VPIH) SHALL CONDUCT AN INDEPENDENT INSPECTION TO CONFIRM THE AREA HAS BEEN PROPERLY CLEANED. AFTER SUCCESSFUL VISUAL INSPECTION BY THE CPIH AND VPIH, FINAL CLEARANCE AIR SAMPLING PROCEDURES WILL BE CONDUCTED PER SPECIFICATION SECTION 02 82 11, ARTICLE 3.6.4.
5. ACM AND LEAD-BASED PAINT DISPOSAL DOCUMENTATION MUST BE SUBMITTED PRIOR TO RELEASE OF RETAINAGE AND FINAL PAYMENT.
6. ABATEMENT CONTRACTOR SHALL COORDINATE ALL WORK WITH THE VA CONTRACTING OFFICER'S REPRESENTATIVE (COR).
7. SEE KEYED NOTES FOR APPROXIMATE LOCATIONS OF ASBESTOS CONTAINING MATERIALS AND LEAD-BASED PAINT TO BE REMOVED.

KEYED NOTES

- ① NO KNOWN SOURCES OF ACM OR LEAD IN THIS AREA.
- ② ACM (LOOSE VERMICULITE) IS SUSPECTED TO BE IN THE CORES OF CONCRETE BLOCKS. NO TESTING WAS PERFORMED. THE SUSPICION IS BASED ON PREVIOUS WORK IN SIMILAR GENERATOR BUILDINGS. PROVIDE ABATEMENT PROCEDURES FOR ALL CORES.
- ③ IN TRAMWAY TUNNEL THE EXISTING HPS, LPS TO TRAMWAY HEATERS ABOVE, AND LPC FROM UNIT HEATERS ABOVE - THESE PIPES HAVE ASBESTOS INSULATION - DO NOT DISTURB - THE INSULATION IS STABLE UNLESS PUNCTURED OR ITS SURFACE BROKEN.
- ④ IN B406 THE CRAWL SPACE DIRT WAS CLEARED OF ACM IN A 2022 PROJECT AND THE PIPE WAS CLEAR PRIOR TO THAT DATE.

LEGEND

SUSPECTED AREA OF HAZARDOUS MATERIALS ABATEMENT

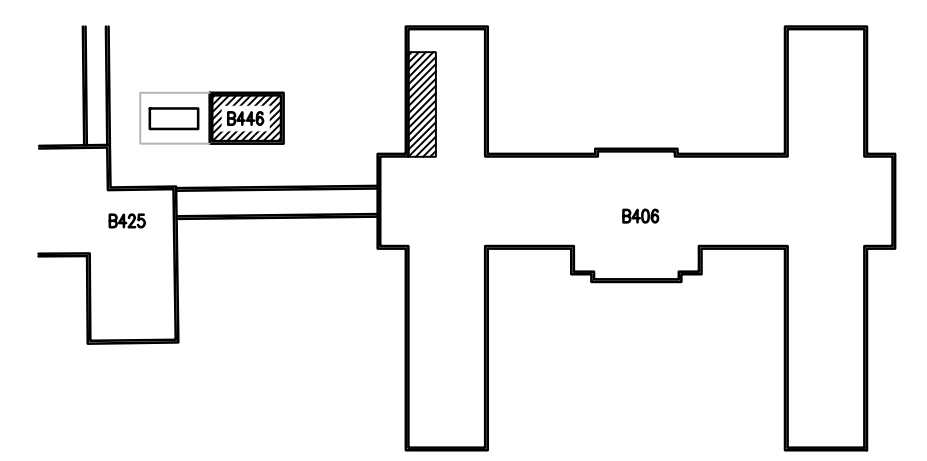

KEY PLAN NORTH

FULLY SPRINKLERED
100% BD DOCUMENT

 VETERANS AFFAIRS MEDICAL CENTER 500 E VETERANS ST TOMAH, WI 54660		CONSULTANTS:	PROJECT LEADER: DESIGN / BUILD SERVICES 1021 N. Superior, Unit 11 Tomah, Wisconsin 54660	Drawing Title HAZARDOUS MATERIALS OVER-ALL FLOOR PLANS	Project Title Connect B406 AHU-5 to Emergency Power	Project Number 676-22-108	Office of Facilities Management
				Approved: Project Director	Location Tomah, Wisconsin	Building Number 446/406	
Revisions:	Date			Date November 20, 2025	Checked By: HFB	Drawn By: KAB	Department of Veterans Affairs

EQUIPMENT		ELECTRICAL DATA		STARTER										DISCONNECT AT UNIT				NOTES									
				TYPE										FURN. BY													
										FURN. BY		ACCESSORIES				FURN. BY											
TAG	SERVES	HP	KW	VOLTAJE	PHASE	MANUAL	MAGNETIC	COMBINATION	VFD	LOCATION	EQUIPMENT MFR	MECHANICAL CONTR.	ELEC. CONTRACTOR	HAND-OFF-AUTO	PILOT LIGHT	PUSH BUTTON	TWO-SPEED	REDUCED VOLTAGE	NOT REQUIRED	WEATHERPROOF	ELEC. CONTRACTOR	FUSED	EQUIPMENT MFR	MECHANICAL CONTR.	ELEC. CONTRACTOR	EMERGENCY POWER	
446-ACCU-1	ELECTRICAL CONTROL ROOM	1	208	1	X	X				ON UNIT	1		1	1	1	1	1	1	X		X	X	1		1	2, 3,	

AIR COOLED CONDENSING UNIT SCHEDULE (ACCU-)

NOTES:

1. BASIS OF DESIGN: ACCU MITSUBISHI PUYAK48NL.
2. BASIS OF DESIGN: FOU MITSUBISHI PLA-AE48NL.
3. PROVIDE LOW AMBIENT KIT TO "2".
4. CONDENSING UNIT INCLUDES A TWIN ROTARY COMPRESSOR.
5. INDOOR UNIT POWERED FROM OUTDOOR UNIT.
6. PROVIDE WIRED THERMOSTAT CONTROL (7 DAY PROGRAMMABLE) WITH COMPATIBLE WIRING KIT.
7. PROVIDE MANUFACTURERS REFRIGERANT LINE SET 5/8" GAS AND 3/8" LIQUID. PROVIDE INSULATION ON BOTH LIQUID AND GAS LINES. PROVIDE ALUMINUM WEATHERPROOF GUARDS AT EXTERIOR.
8. PROVIDE HAIL GUARD ON CONDENSING UNIT.
9. PROVIDE BACNET AND MODBUS PROTOCOL INTERFACE.

[illegible]


1. SEE SHEET M001 FOR NOTES, LEGEND, AND ABBREVIATIONS.
2. COORDINATE WITH ALL DISCIPLINES BEFORE CONSTRUCTION.
3. SUBMITTAL APPROVED COORDINATION DRAWINGS ARE REQUIRED BEFORE ANY CONSTRUCTION WORK MAY START.
4. SEE GENERAL SHEETS FOR PHASING, FOLLOW ALL PHASING REQUIREMENTS.

- ① PROVIDE NEW SPLIT SYSTEM AIR CONDITIONING UNIT, MOUNT EVAPORATOR UNIT (INDOOR FUC-1) TO WALL AT 96" AFF AND CENTERED OVER DOOR, ROUTE CONDENSATE DRAIN TO EXTERIOR AS NOTED.
- ② PROVIDE LINE SET SIZED BY MFR, INSULATE BOTH PIPES, ROUTE UP TO ROOF STRUCTURE, CORE HOLE THRU WALL BETWEEN GENERATOR AND ELECTRICAL ROOM, SEAL ALL—AROUND WITH FIRE RATED 2-HOUR CAULK, CAULKING BY SEALANT MANUFACTURER.
- ③ PIPES SHALL FOLLOW ROOF STRUCTURE TO EXTERIOR WALL, CORE HOLE THRU WALL TO EXTERIOR, PROVIDE A WALL PENETRATION FLASH JACKET OVER INSULATION AT EXTERIOR, SEAL OPENING WITH FIRE RATED 2-HOUR CAULK, CAULKING BY SEALANT MANUFACTURER, ROUTE CONDENSATE DRAIN EXTERIOR WALL TURN TOWARDS CONDENSING UNIT AT 36" ABOVE FINISHED GRADE.
- ④ SUPPORTS PIPES AT ALL ROUTINGS.
- ⑤ 3/4" PVC DRIN (UN PROTECTED), ELBOW DOWN OUTSIDE BUILDING, PROVIDE STAINLESS STEEL SCREEN AT OUTLET TERMINATION, SECURED TO 3/4" PVC.
- ⑥ SECURE TO WALL, ROUTE DOWN TO 24" ABOVE FINISHED GRADE, PROVIDE SCHED 40 STEEL SLEEVE, FILL ALL AROUND DRAIN WITH GROUT FROM EXTERIOR TO INTERIOR.
- ⑦ PROVIDE NEW SPLIT SYSTEM AIR CONDITIONING UNIT, MOUNT CONDENSING UNIT (OUTDOOR ACCU-1) ON NEW CONCRETE PAD, PROVIDE VIBRATION ISOLATORS ON FEET OF CONDENSING UNIT, SECURE TO PAD WITH WEDGE ANCHOR.
- ⑧ PROVIDE SUPPORTS SIMILAR TO RUBBER ROOF SUPPORTS FOR REFRIGERANT PIPING BETWEEN CONDENSING UNIT AND ROUTING ON WALL.
- ⑨ PROVIDE FLEXIBLE HOSE CONNECTIONS FOR REFRIGERATION PIPING AT CONDENSING UNIT.
- ⑩ DROP REFRIGERANT PIPES DOWN 2 COURSES THEN CORE THRU WALL.



PCG
DESIGN / BUILD SERVICES
1021 N. Superior, Unit 11
Tomah, Wisconsin 54660

 Department of
Veterans Affairs

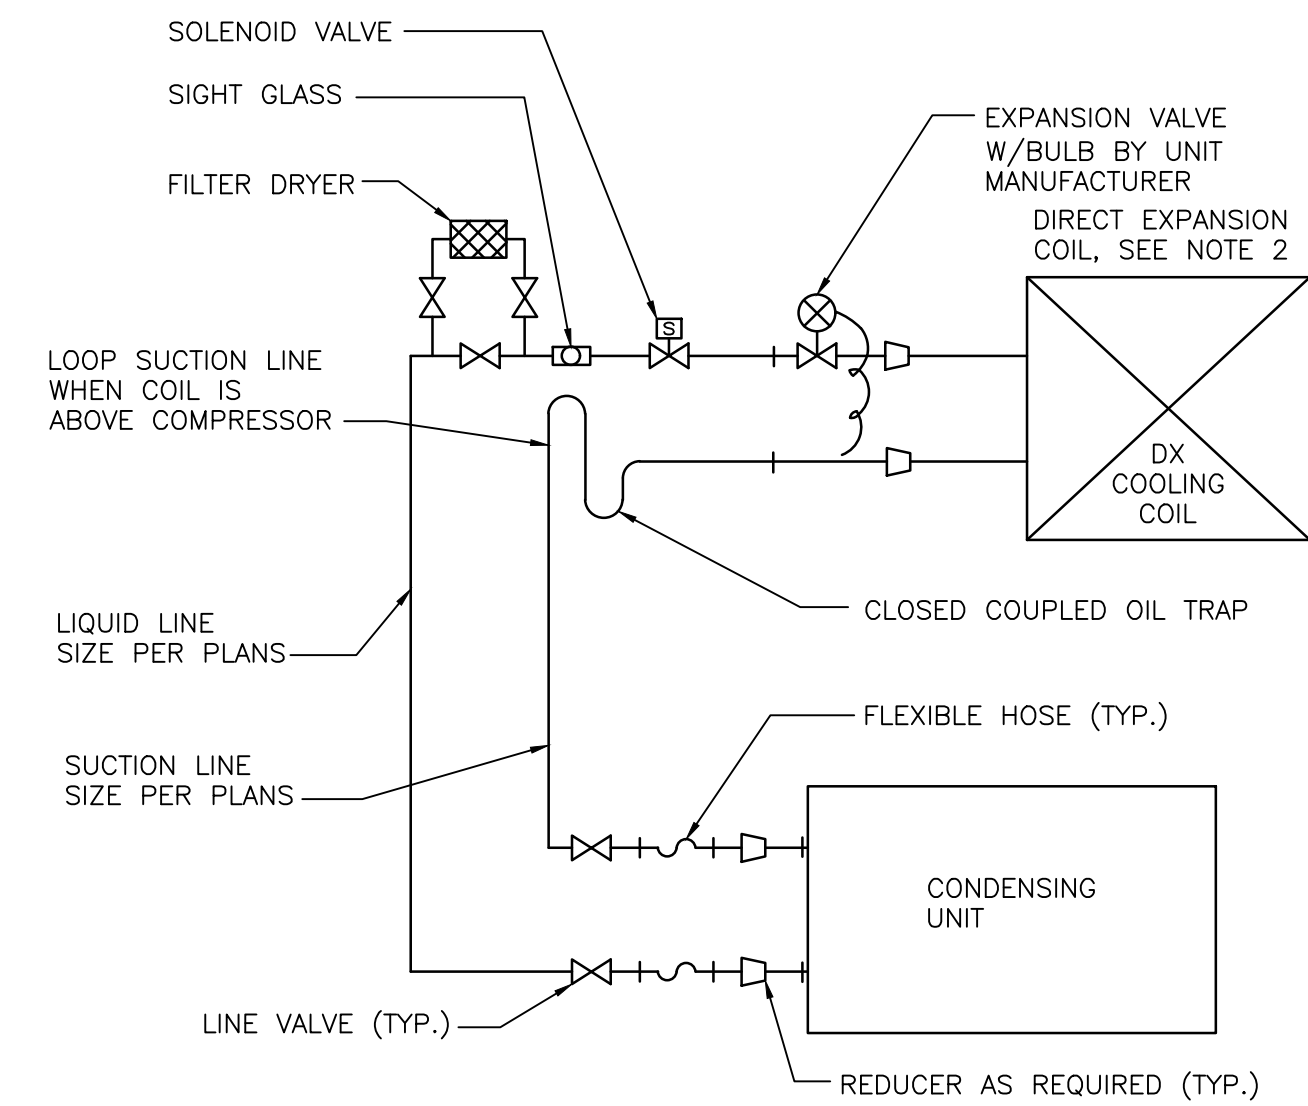

1. CPVC PIPE MAY BE USED ONLY IF APPROVED BY LOCAL VA AND IS INDOORS AND DOES NOT PASS THROUGH RATED BARRIERS.
2. DIELECTRIC FITTING TO BE USED WHEN TWO DISSIMILAR METALS ARE TO BE CONNECTED.
3. TRAP DIMENSIONS NOTED FOR 406-AHU-5 FIT THE STATIC PRESSURE REQUIREMENTS AND WERE PROVIDED BY THE BASIS OF DESIGN MANUFACTURER. ANY CHANGES TO THE STATIC PRESSURE OR MANUFACTURER SHALL BE THE MECHANICAL CONTRACTOR AND SELECTED EQUIPMENT MANUFACTURERS RESPONSIBILITY TO VERIFY TRAP DIMENSIONS.
4. BASIS OF DESIGN AHU SELECTION, $A = 7.5"$ AND $B = 4"$.

1. SINGLE CIRCUIT SHOWN. PIPING TYPICAL FOR EACH OF TWO CIRCUITS.
2. CONDENSATE FROM COOLING COIL SHALL BE TRAPPED AND ROUTED AS INDICATED TO DRAIN.
3. PROVIDE DOUBLE RISER FOR UNITS UNLOADING AT A 25% OR LESS CAPACITY.

4 SPLIT DX SYSTEM REFRIGERANT PIPING DIAGRAM

MAXIMUM PIPE/TUBING SUPPORT SPACING										
NOM. SIZE IN.	THRU 3/4	1	1 1/4	1 1/2	2	2 1/2	3	4	5	6
PIPE FT.	7	7	9	10	11	12	14	16	17	
TUBING FT.	5 FT	6	7	8	8	9	10	12	13	14

NOTE: FOR TRAPEZE HANGER TAKE SPACING OF SMALLEST SIZE ON TRAPEZE.

GENERAL NOTES

1. SEE SHEET E001 FOR NOTES, LEGEND, AND ABBREVIATIONS.
2. SEE SHEET GC103 FOR PHASING REQUIREMENTS.
3. SEE SHEET CD101 FOR SITE REQUIREMENTS.

KEYED NOTES

- ① DISCONNECT EXISTING WIRING FROM CHILLER.
- ② DISCONNECT EXISTING FEEDER FROM CHILLER ALL THE WAY BACK TO EXISTING MDP. ALL WIRING, CONDUIT, AND SUPPORTS ARE ONLY REMOVED UP TO END OF RUN IN TRAMWAY TUNNEL BEFORE GOING UNDERGROUND, AND ONLY AFTER NEW CONDUIT AND CONDUCTORS ARE INSTALLED, CONNECTED, AND FULLY FUNCTIONAL. PROVIDE CAP OVER 3" OPENING AT THE EXISTING PULL BOX. REMOVE THE REST OF THE 3" CONDUIT UNDER THE TRAMWAY AND ALL FITTINGS BACK TO THE MDP.
- ③ ABANDON EXISTING UNDERGROUND 3" CONDUIT AS A SPARE.
- ④ CUT EXISTING CONDUIT AT GROUND LEVEL. REMOVE CONDUCTORS. CAP WITH WATERTIGHT CAP FOR FUTURE USE.
- ⑤ PROVIDE 9"x6" ALUMINUM SIGN, RED BACKGROUND WITH WHITE LETTERING, REFLECTIVE BORDER, "3" ABANDONED CONDUIT TO CHILLER," SECURE TO PULL BOX WITH 2 - 3/16" x 1/4" SHEET-METAL SCREWS.

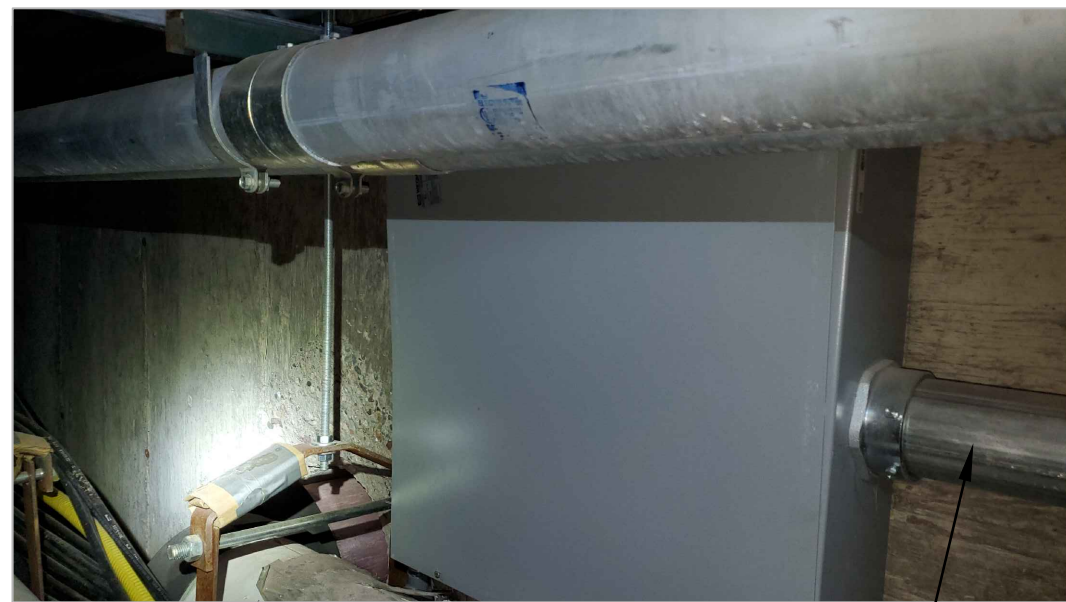


PHOTO 1



PHOTO 2

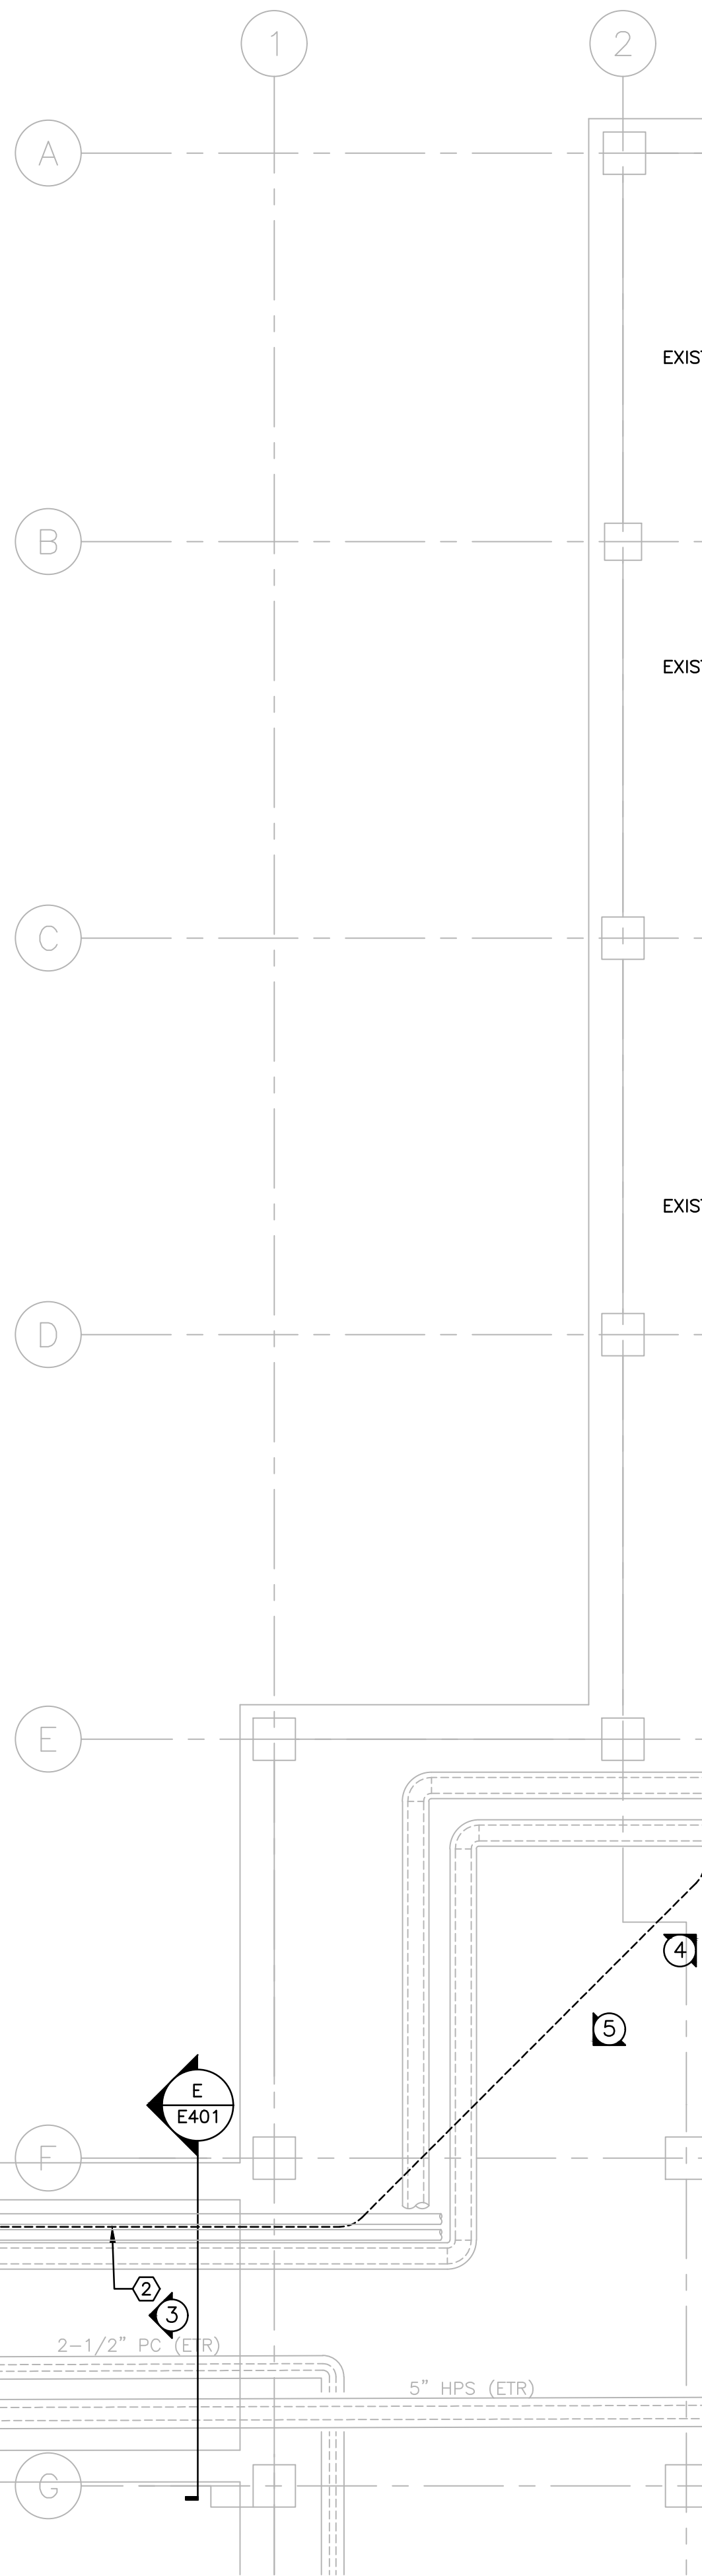


PHOTO 3



PHOTO 4


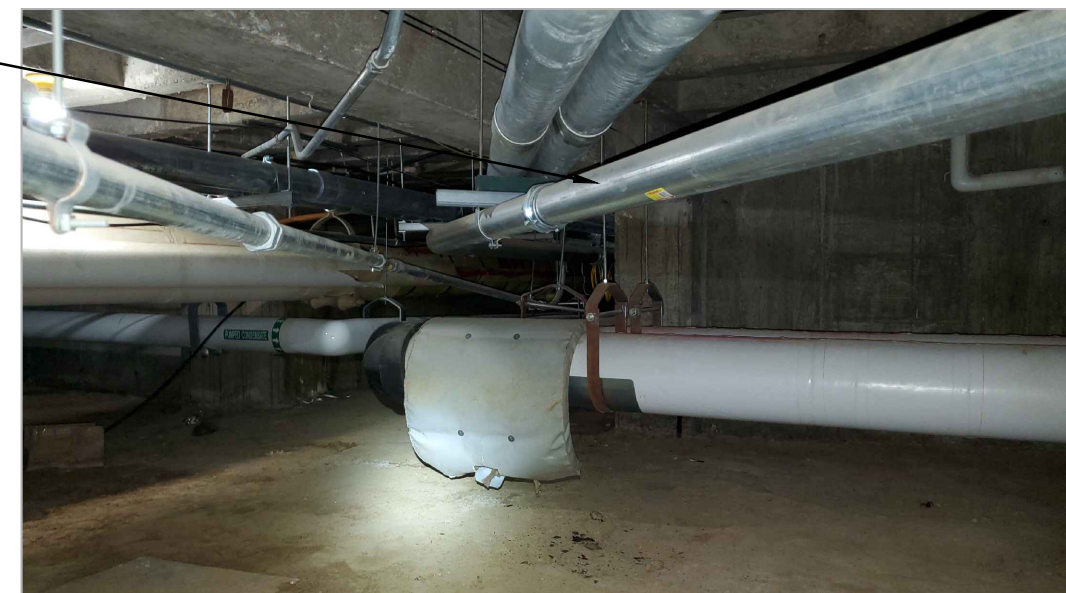


PHOTO 5

1 B406 UTILITY TUNNEL/UNDERGROUND PLAN
1/4"= 1'-0"

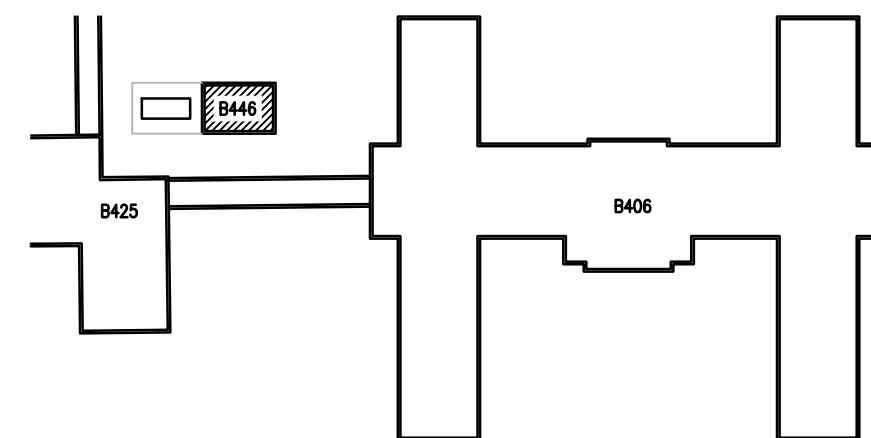

KEY PLAN NORTH

FULLY SPRINKLERED
100% BD DOCUMENT

Revisions:	Date



VETERANS AFFAIRS
MEDICAL CENTER
500 E VETERANS ST
TOMAH, WI 54660



CONSULTANTS:

PROJECT LEADER:



Drawing Title
ELECTRICAL - B406 UTILITY
TUNNEL/ UNDERGROUND PLAN
- DEMOLITION

Approved: Project Director

Project Title
Connect B406 AHU-5 to
Emergency Power

Location
Tomah, Wisconsin

Date
November 20, 2025

Checked By:
HFB

Drawn By:
SJS

Project Number
676-22-108
Building Number
446/406

Drawing Number
ED101

Office of
Facilities
Management



three inches = one foot
one and one half inches = one foot
one inch = one foot
three quarters inch = one foot
one half inch = one foot
three eighths inch = one foot
one quarter inch = one foot
one eighth inch = one foot

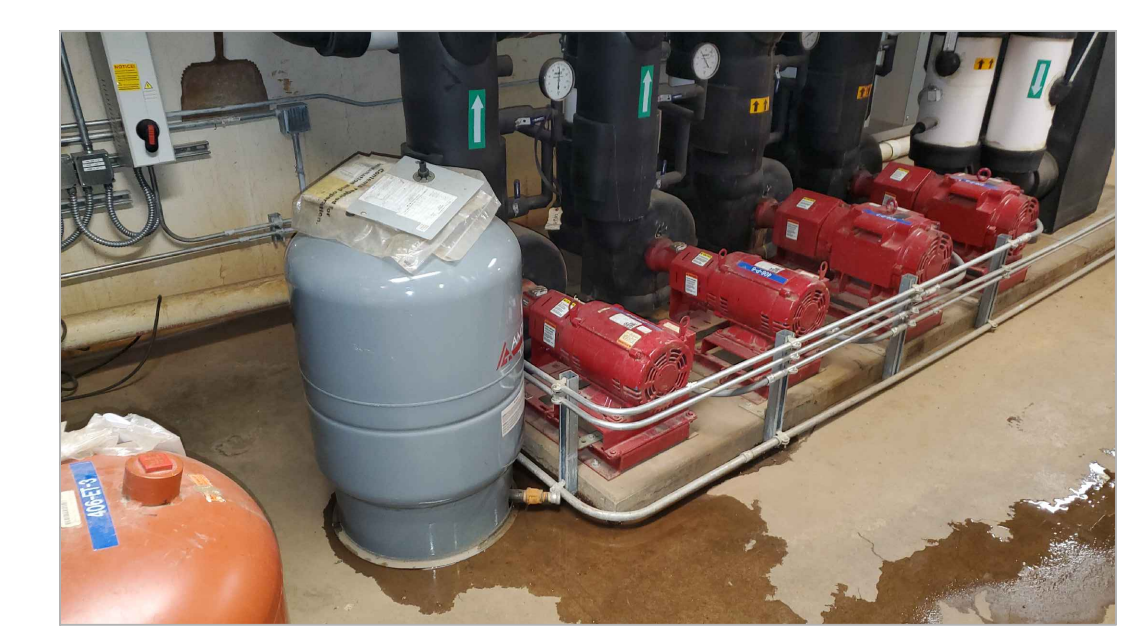
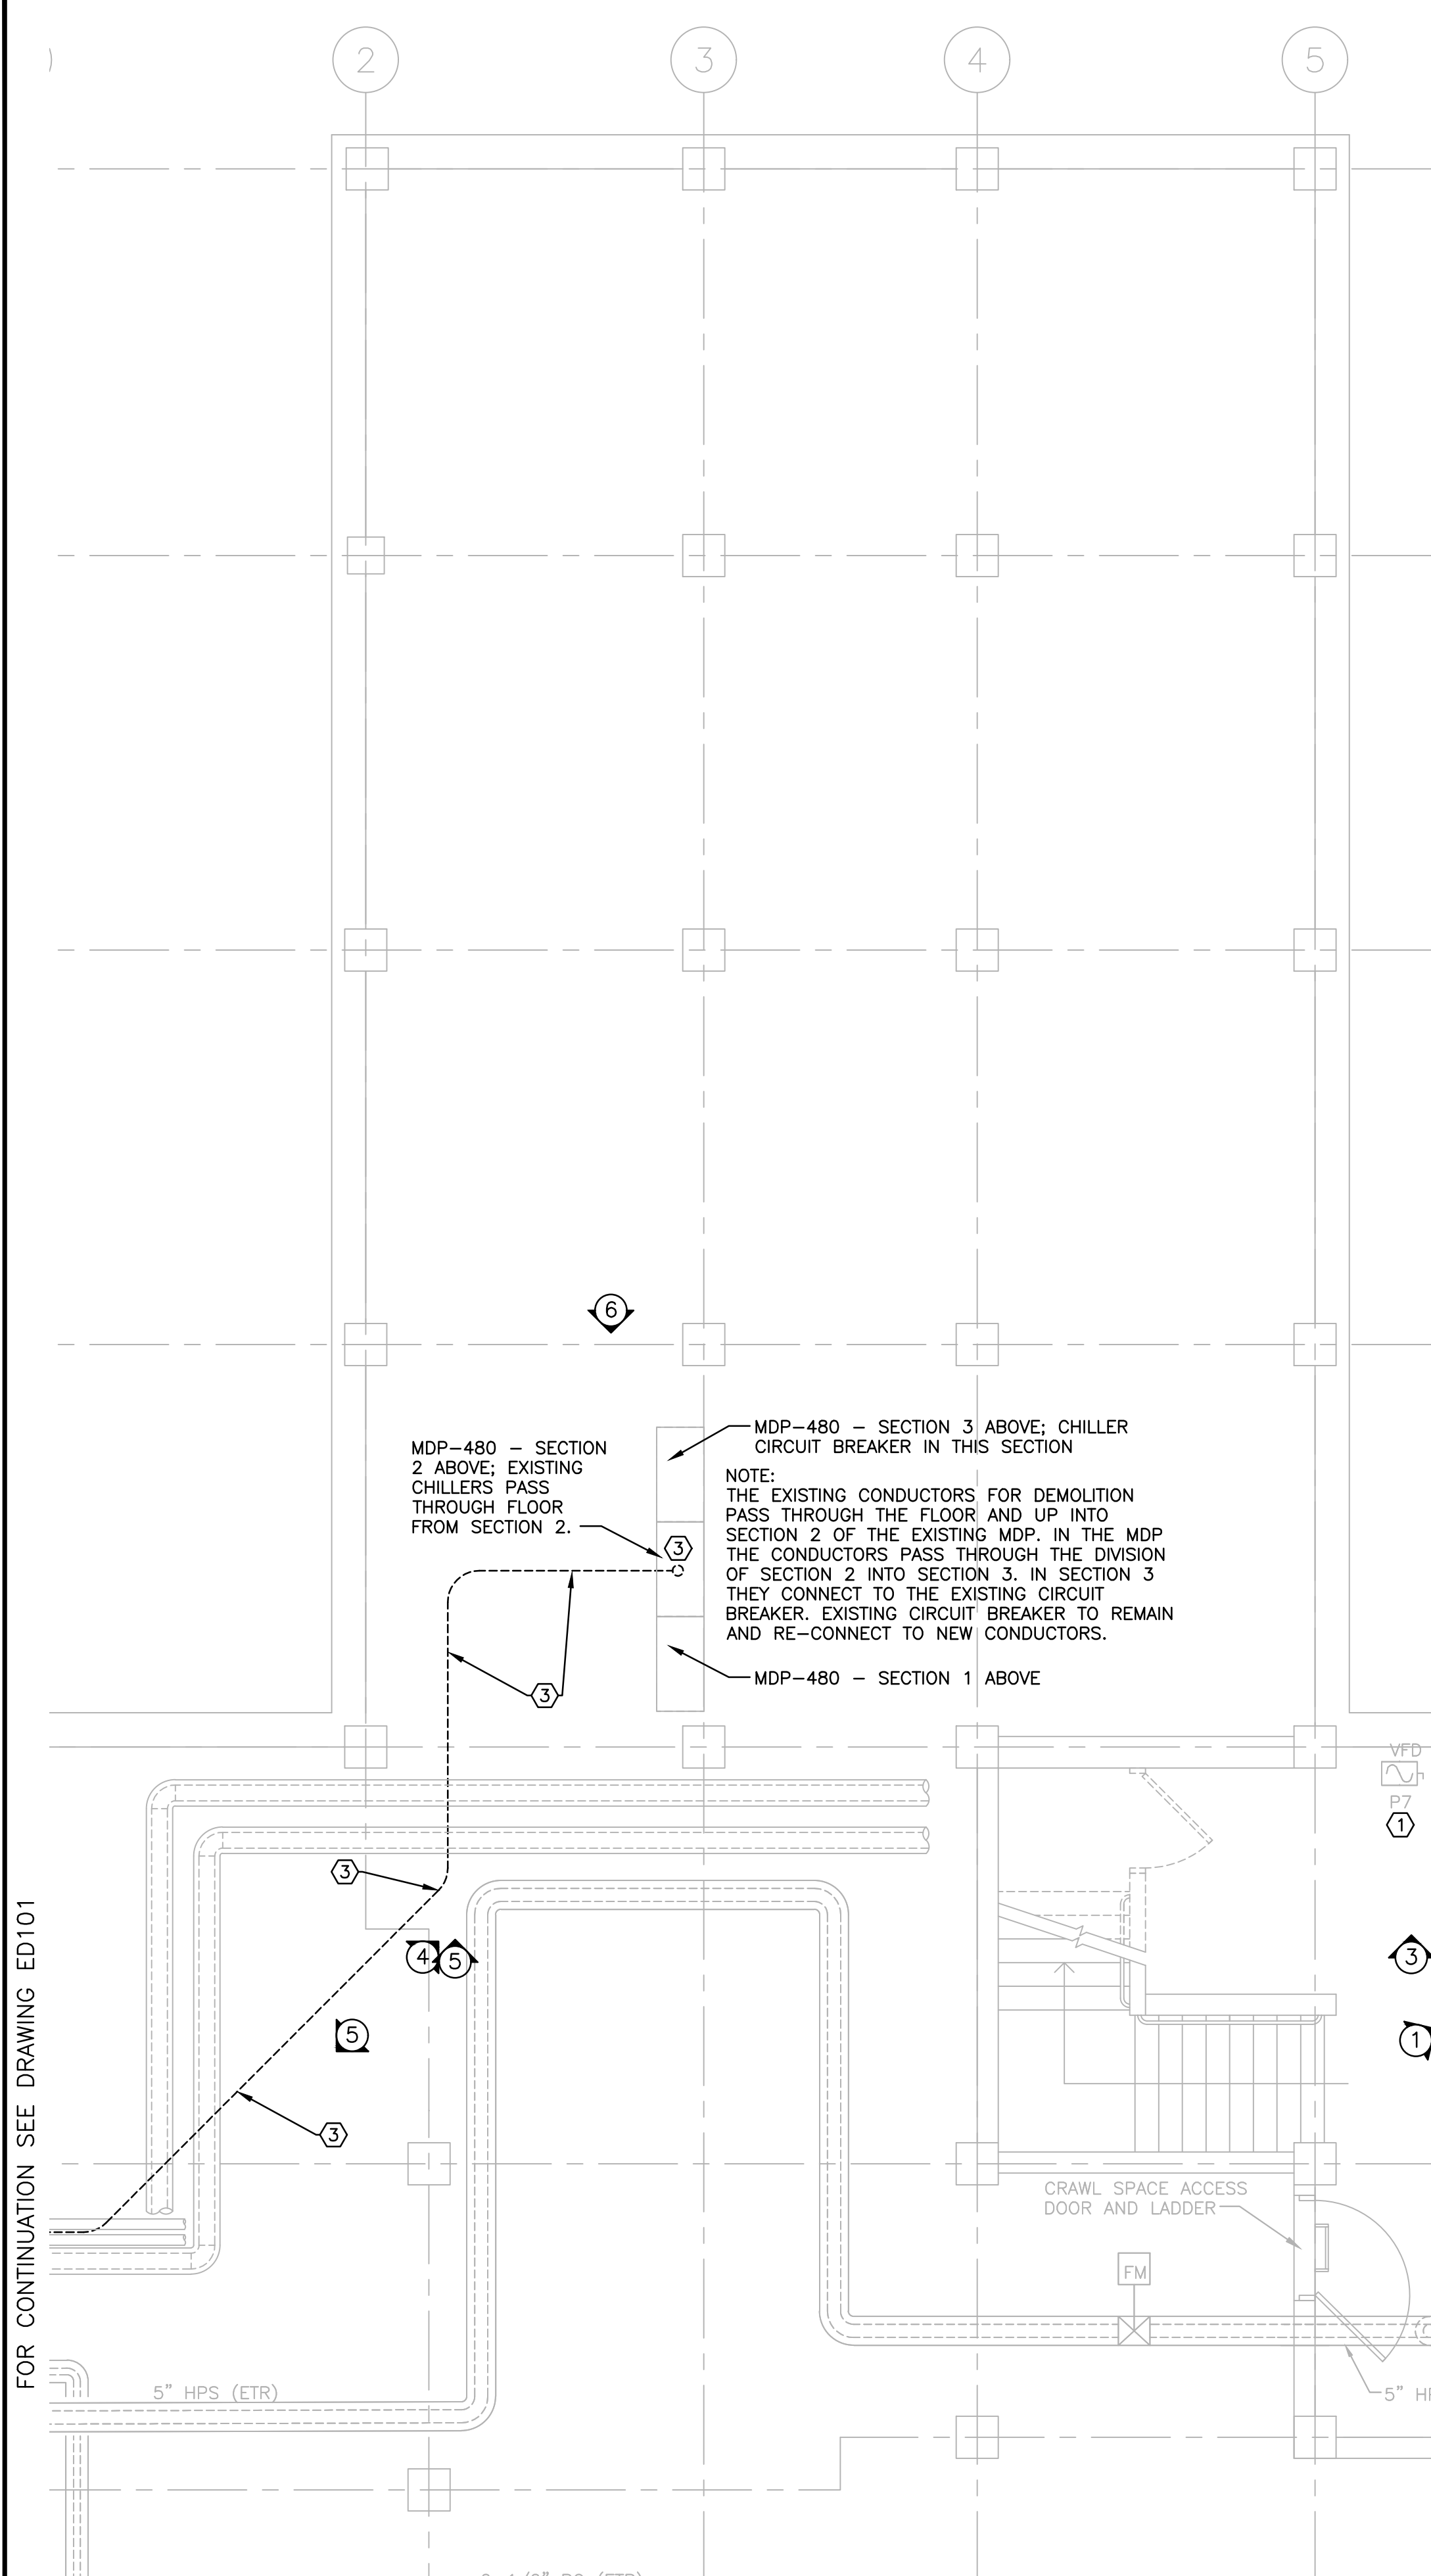


PHOTO 1



PHOTO 2

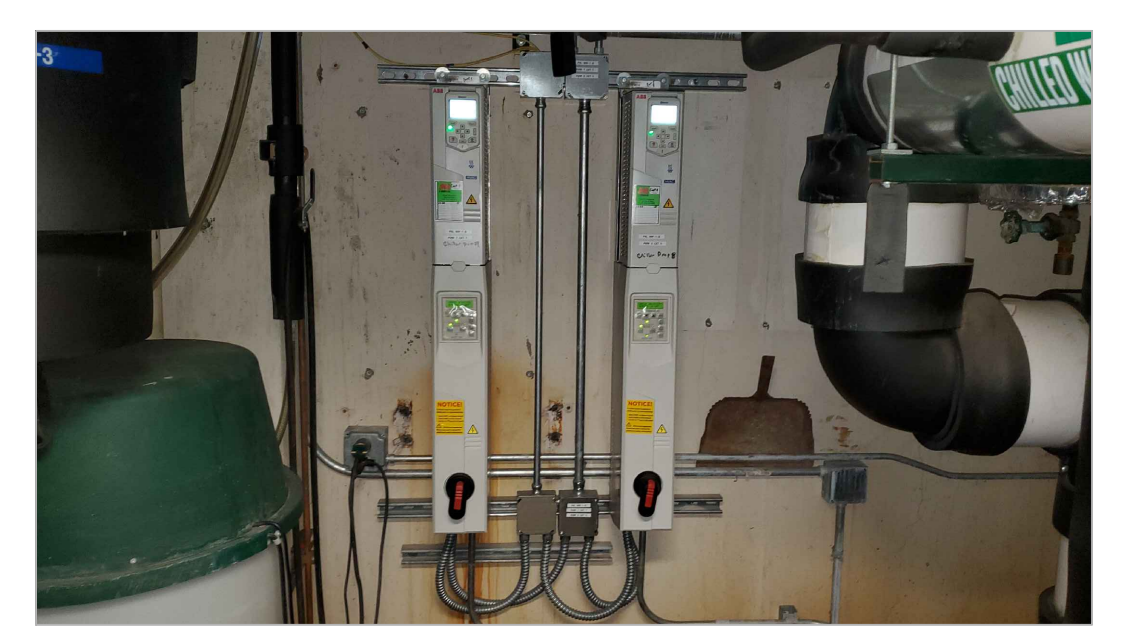


PHOTO 3

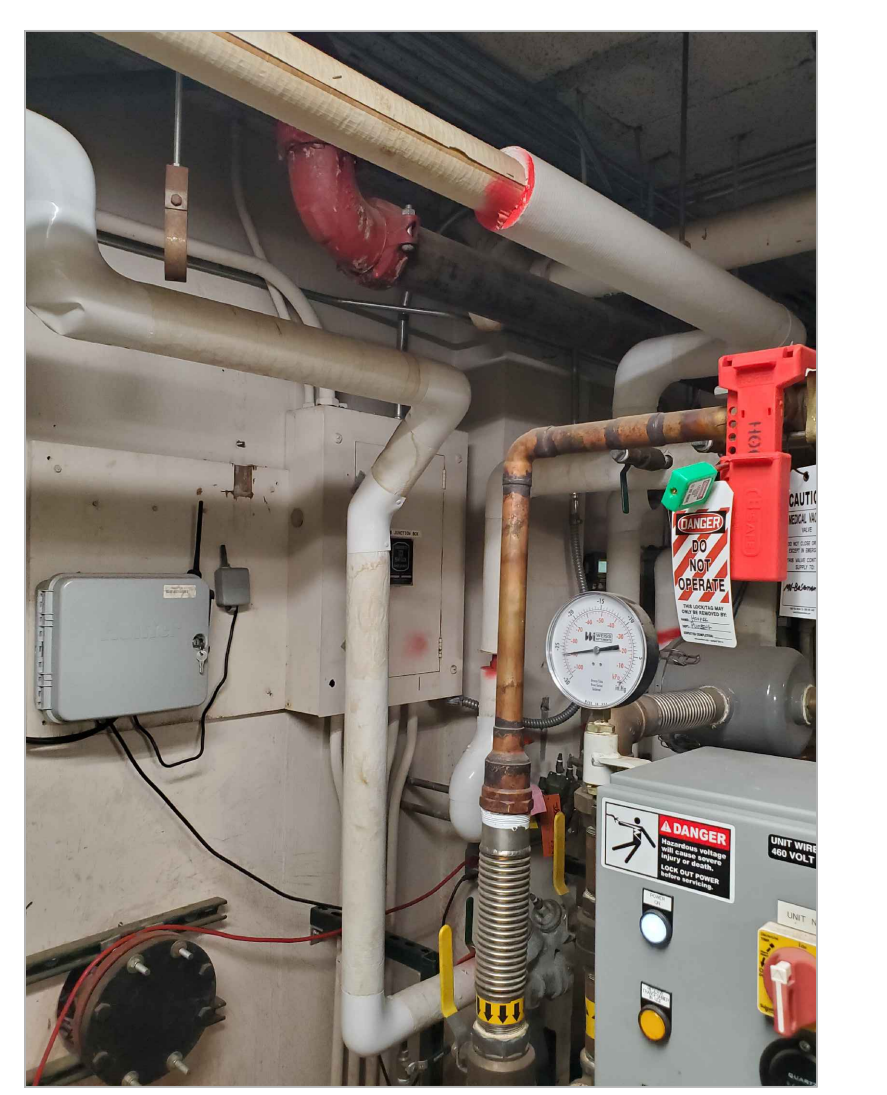


PHOTO 4

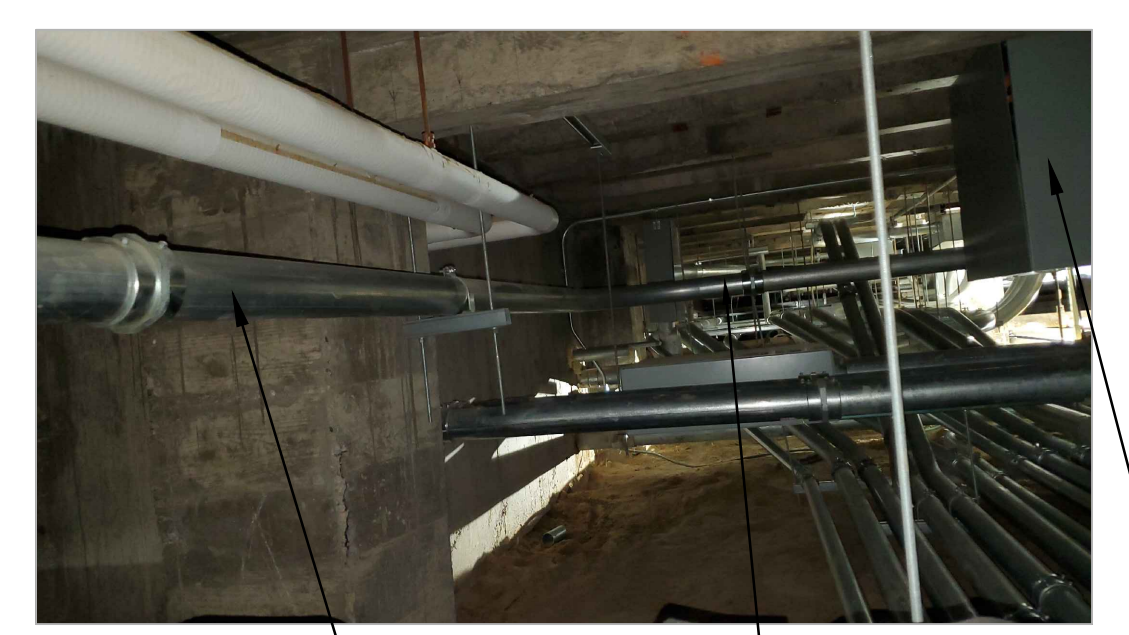


PHOTO 5

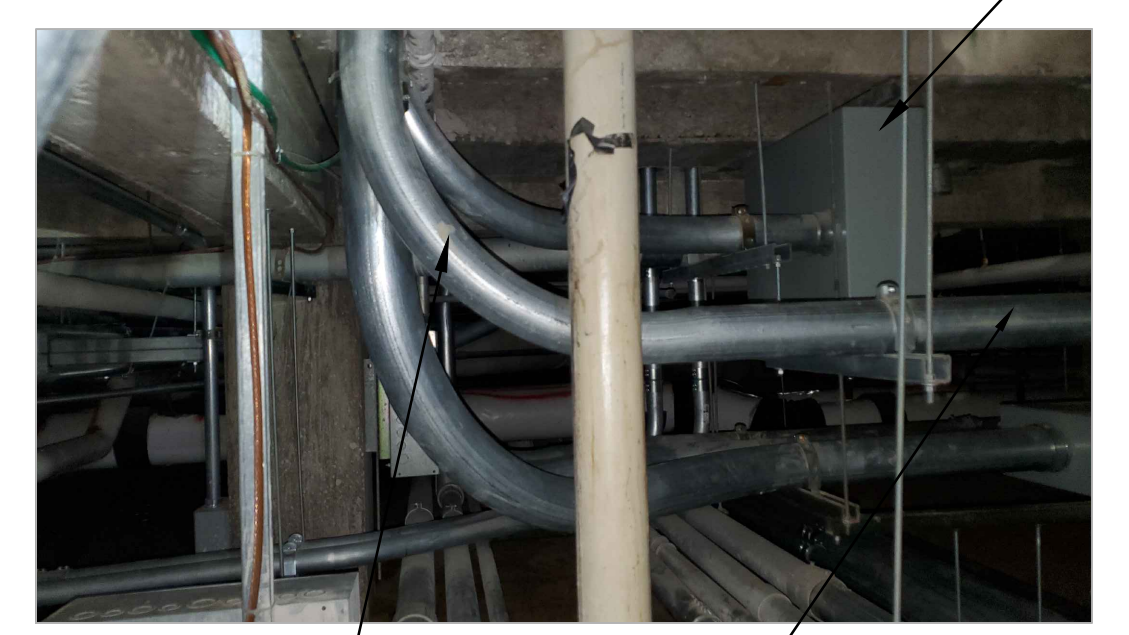


PHOTO 6


GENERAL NOTES:
1. SEE SHEET E001 FOR NOTES, LEGEND, AND ABBREVIATIONS.
2. SEE SHEET GC103 FOR PHASING REQUIREMENTS.

KEYED NOTES:
① DISCONNECT EXISTING PUMPS. MAINTAIN EXISTING WIRING AND CONDUIT FROM PUMPS TO EXISTING VFDS. REMOVE EXISTING CONDUIT AND WIRE FROM VFDS TO EXISTING PANEL. PREPARE FOR EXTENSION OF NEW CIRCUIT TO PUMP AND VFD.
② RELOCATE EXISTING CTRL. PANEL FOR INSTALLATION OF NEW EMERGENCY PANEL. IDENTIFY PANEL AND COORDINATE WITH VA CCR FOR NEW LOCATION. PROVIDE NEW JUNCTION BOX AND CABLE TO MATCH EXISTING CABLE FOR PANEL.
③ DISCONNECT EXISTING FEEDER FROM CHILLER ALL THE WAY BACK TO EXISTING MDP. REMOVE ALL WIRING CONDUIT TO ONLY BE REMOVED UP TO END OF RUN IN TRAMWAY BEFORE GOING UNDERGROUND. CUT, CAP, AND SEAL. REMOVE 3" CONDUIT UNDER TRAMWAY AND ALL FITTINGS BACK TO MDP.

EXISTING MOTOR REFERENCE INFORMATION:
P5 MOTOR: FRAME 213/ST, INS. CL. F, ODP, INV. DUTY, 10 HP, 480V, 3PH, 60HZ, 1765 RPM, PREMIUM MOTOR, JUNE 13, 2007.
P6 MOTOR: FRAME 213/ST, INS. CC. F, ODP, INV. DUTY, 10 HP, 480V, 3PH, 60HZ, 1765 RPM, PREMIUM MOTOR, JUNE 13, 2007.
P7 MOTOR: FRAME 254T, INS. CL. F, ODP, INV. DUTY, 15HP, 480V, 3PH, 60HZ, 1775 RPM, PREMIUM MOTOR, JUNE 13, 2006.
P8 MOTOR: FRAME 254T, INS. CL. F, ODP, INV. DUTY, 15HP, 480V, 3PH, 60HZ, 1775 RPM, PREMIUM MOTOR, JUNE 13, 2006.



MDP-480 - SECTION 2 ABOVE; EXISTING CHILLERS PASS THROUGH FLOOR FROM SECTION 2.
MDP-480 - SECTION 3 ABOVE; CHILLER CIRCUIT BREAKER IN THIS SECTION
NOTE: THE EXISTING CONDUCTORS FOR DEMOLITION PASS THROUGH THE FLOOR AND UP INTO SECTION 2 OF THE EXISTING MDP. IN THE MDP THE CONDUCTORS PASS THROUGH THE DIVISION OF SECTION 2 INTO SECTION 3. IN SECTION 3 THEY CONNECT TO THE EXISTING CIRCUIT BREAKER. EXISTING CIRCUIT BREAKER TO REMAIN AND RE-CONNECT TO NEW CONDUCTORS.
MDP-480 - SECTION 1 ABOVE

1 CRAWLSPACE/ MECHANICAL ROOM PLAN
1/4"= 1'-0"
NORTH

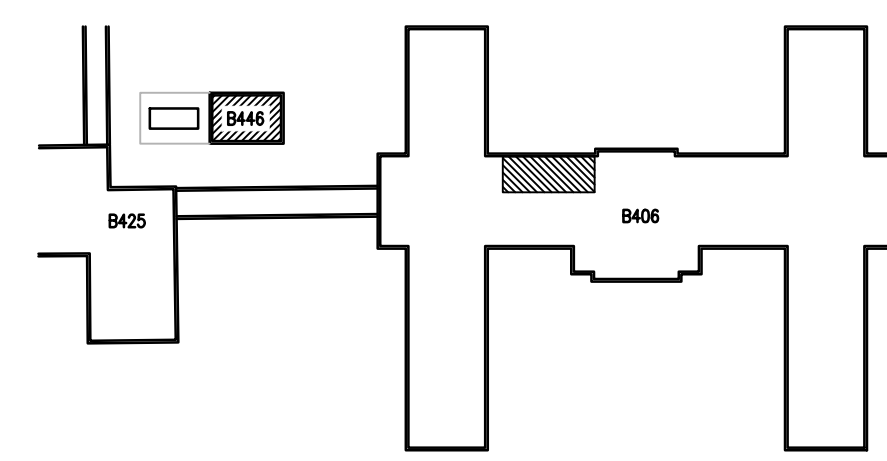

KEY PLAN NORTH
FULLY SPRINKLERED
100% BD DOCUMENT

--	--	

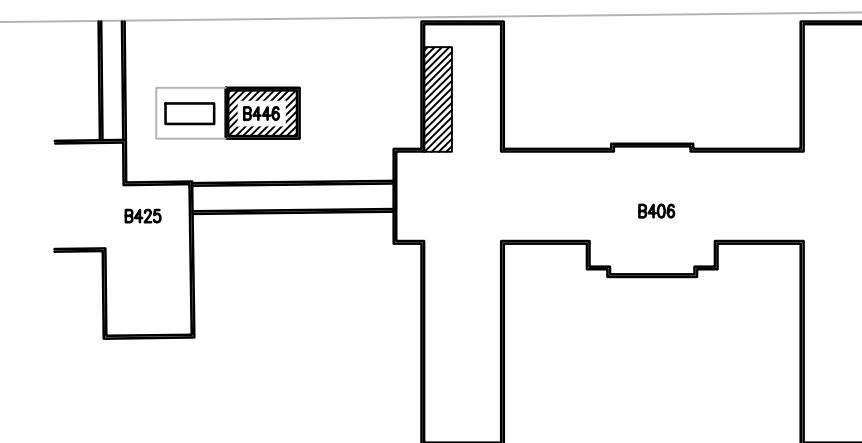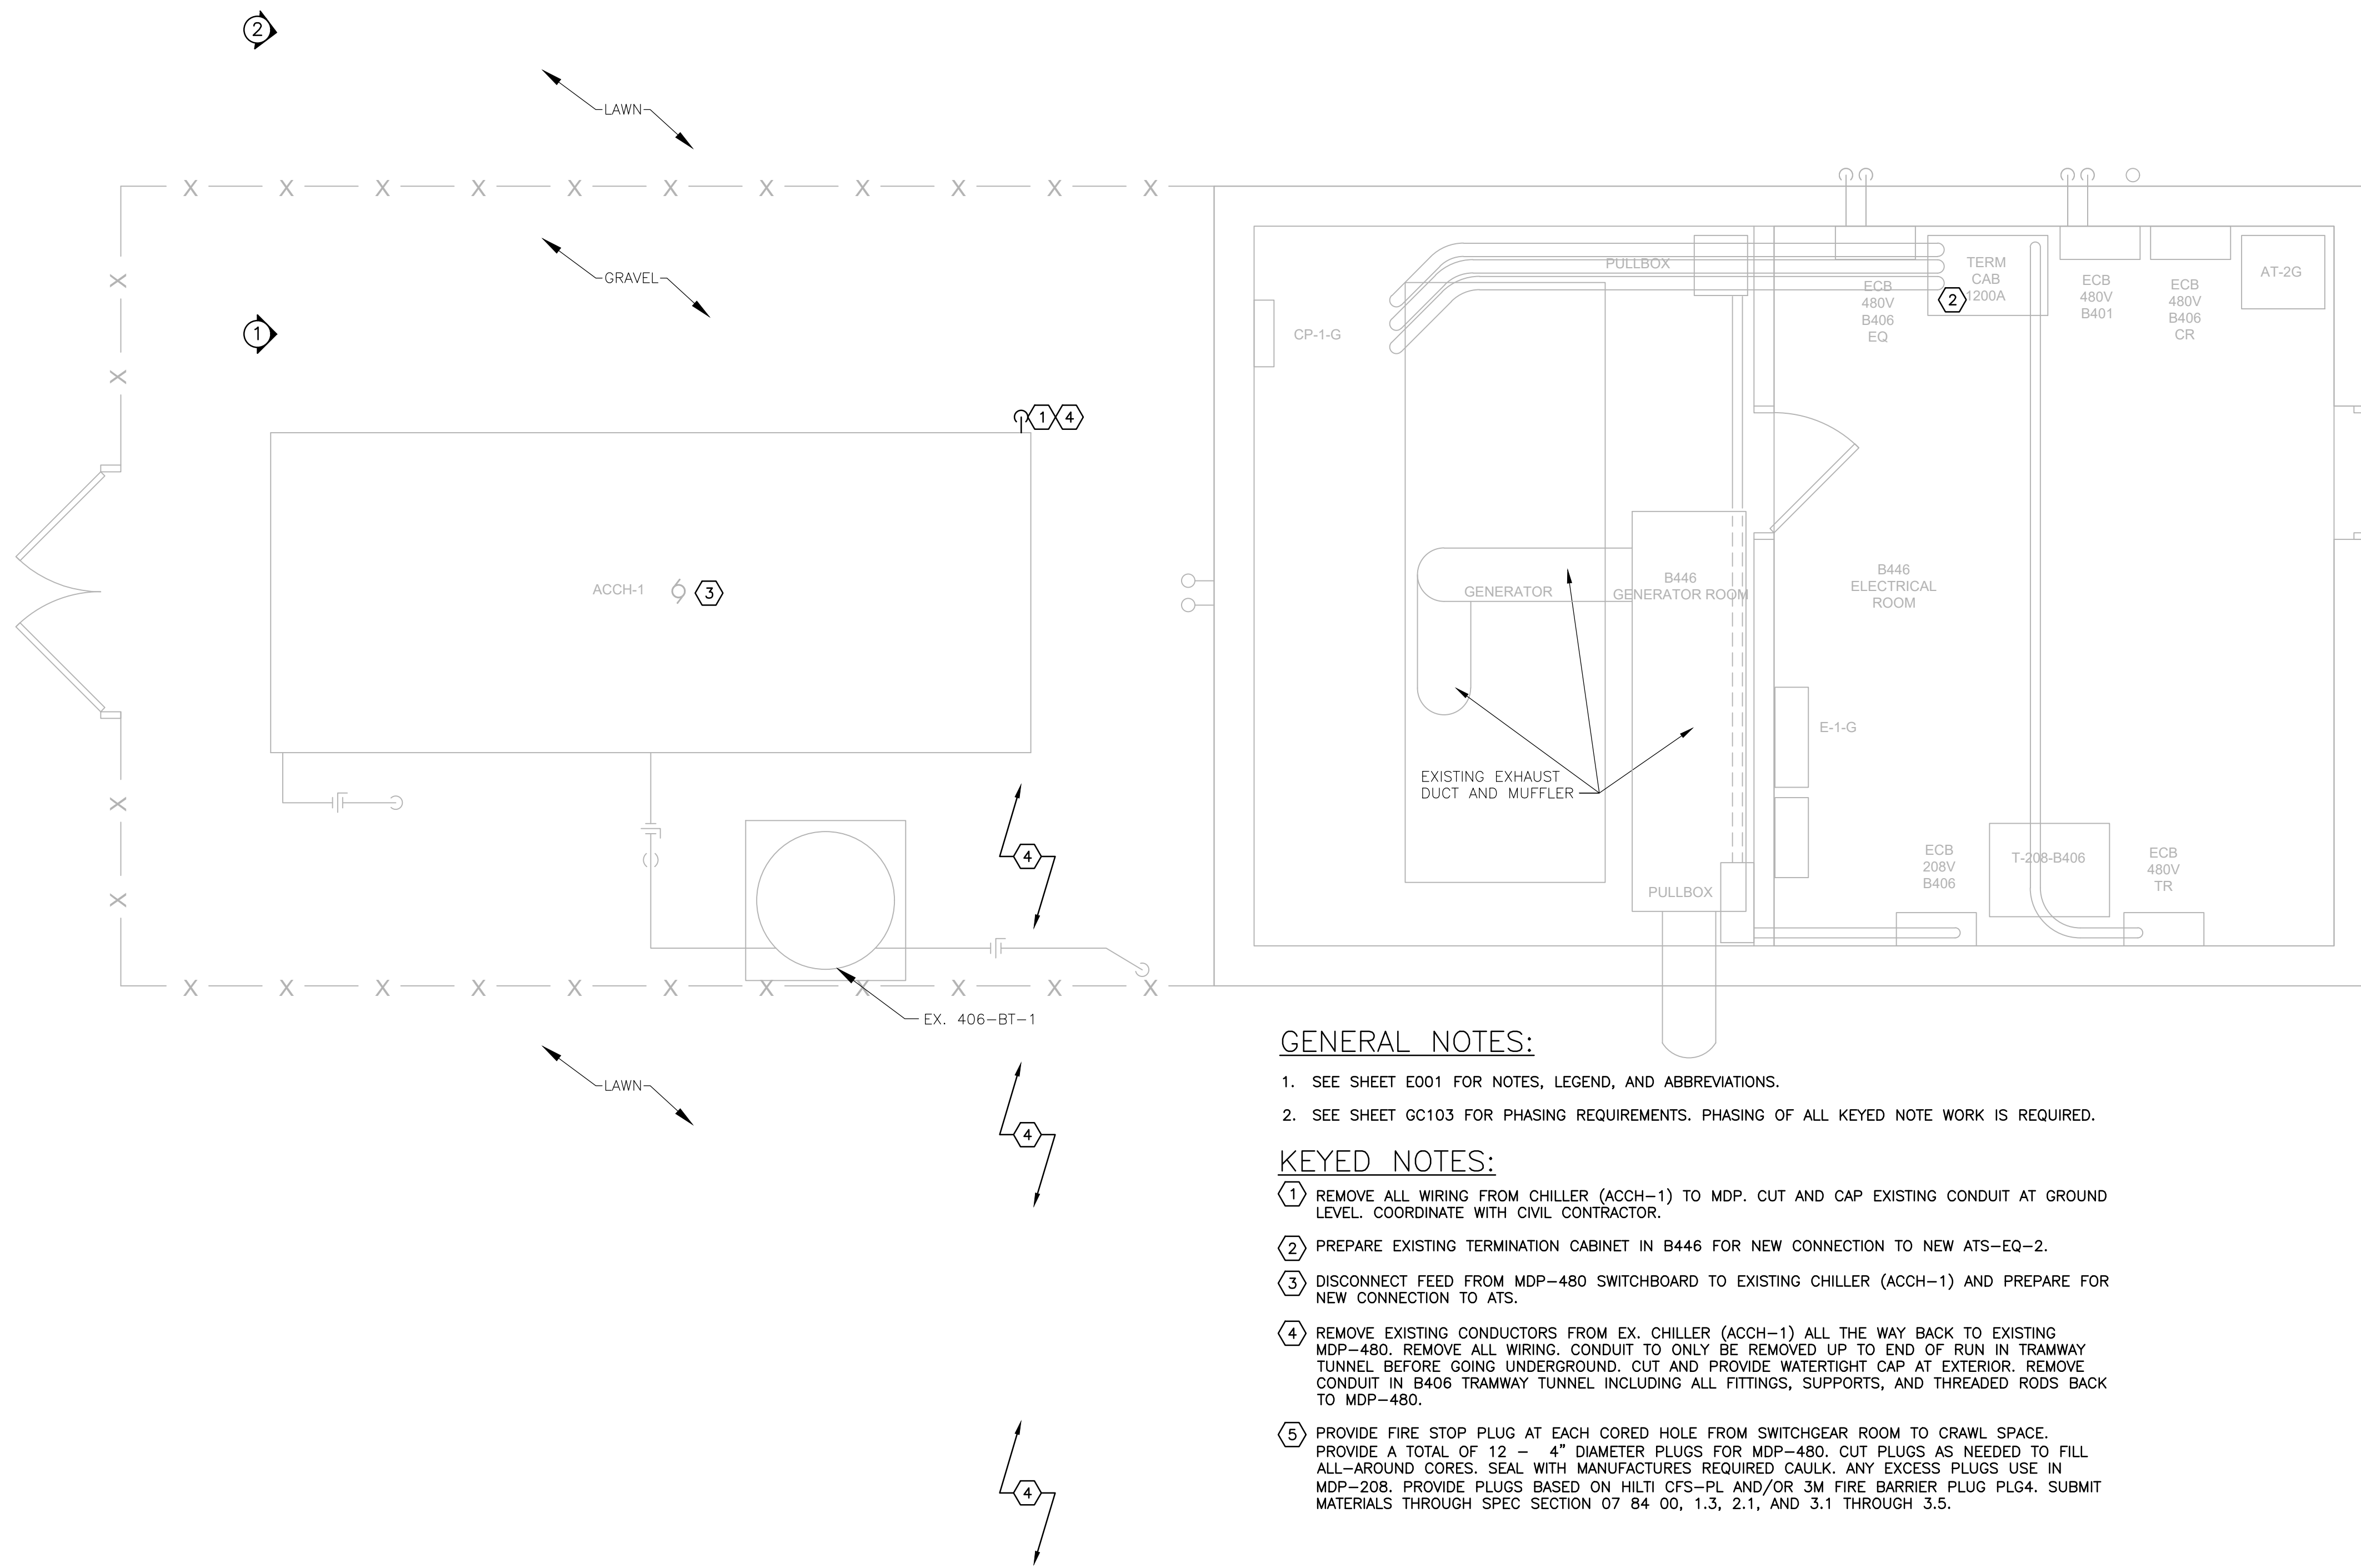

KEY PLAN  NORTH

FULLY SPRINKLERED
100% BD DOCUMENT

[illegible]

CONSULTANTS:

PROJECT LEADER:



Drawing Title	ELECTRICAL B446/B406 PARTIAL FIRST FLOOR PLAN - DEMOLITION
---------------	--

Approved: Project Director

Project Title	Connect B406 AHU-5 to Emergency Power
---------------	--

	Location Tomah, Wisconsin

Date
November 20, 2025

5	Checked By HFB
---	-------------------


Drawn By:	SJS
-----------	-----


Project Number	676-22-108
Building Number	446/406










Drawing Number	ED103
----------------	-------

Office of
Facilities
Management



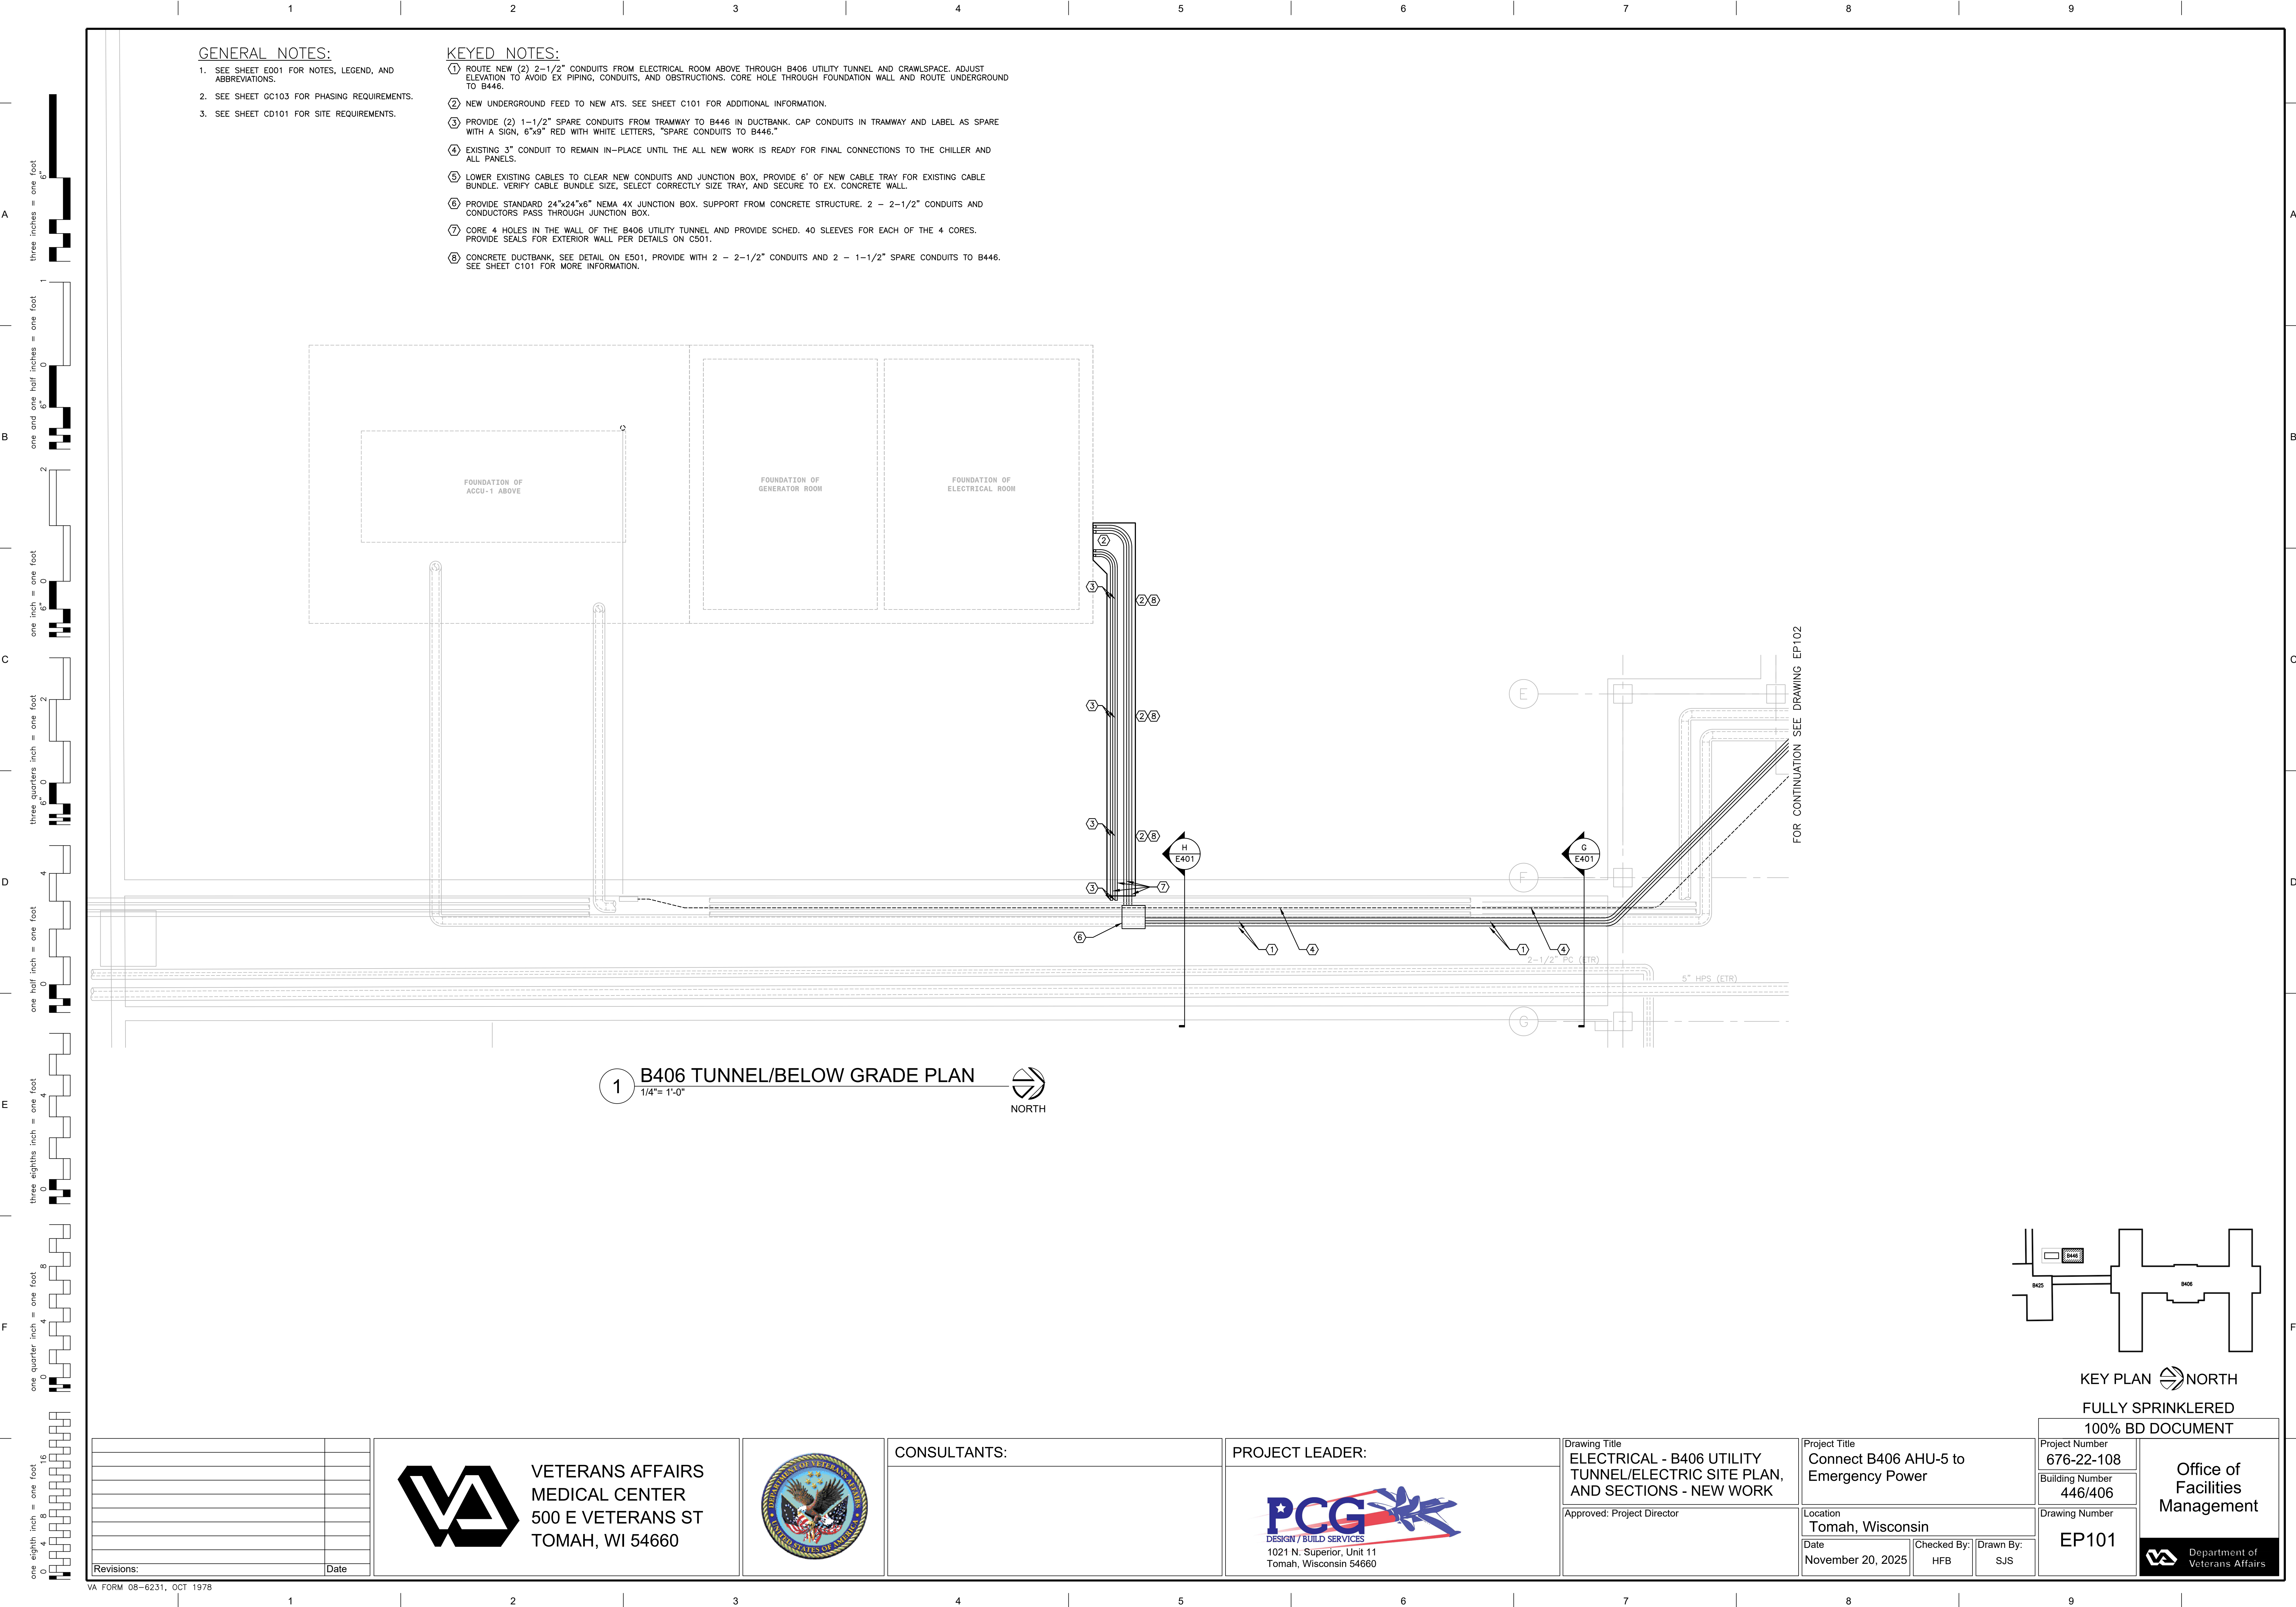

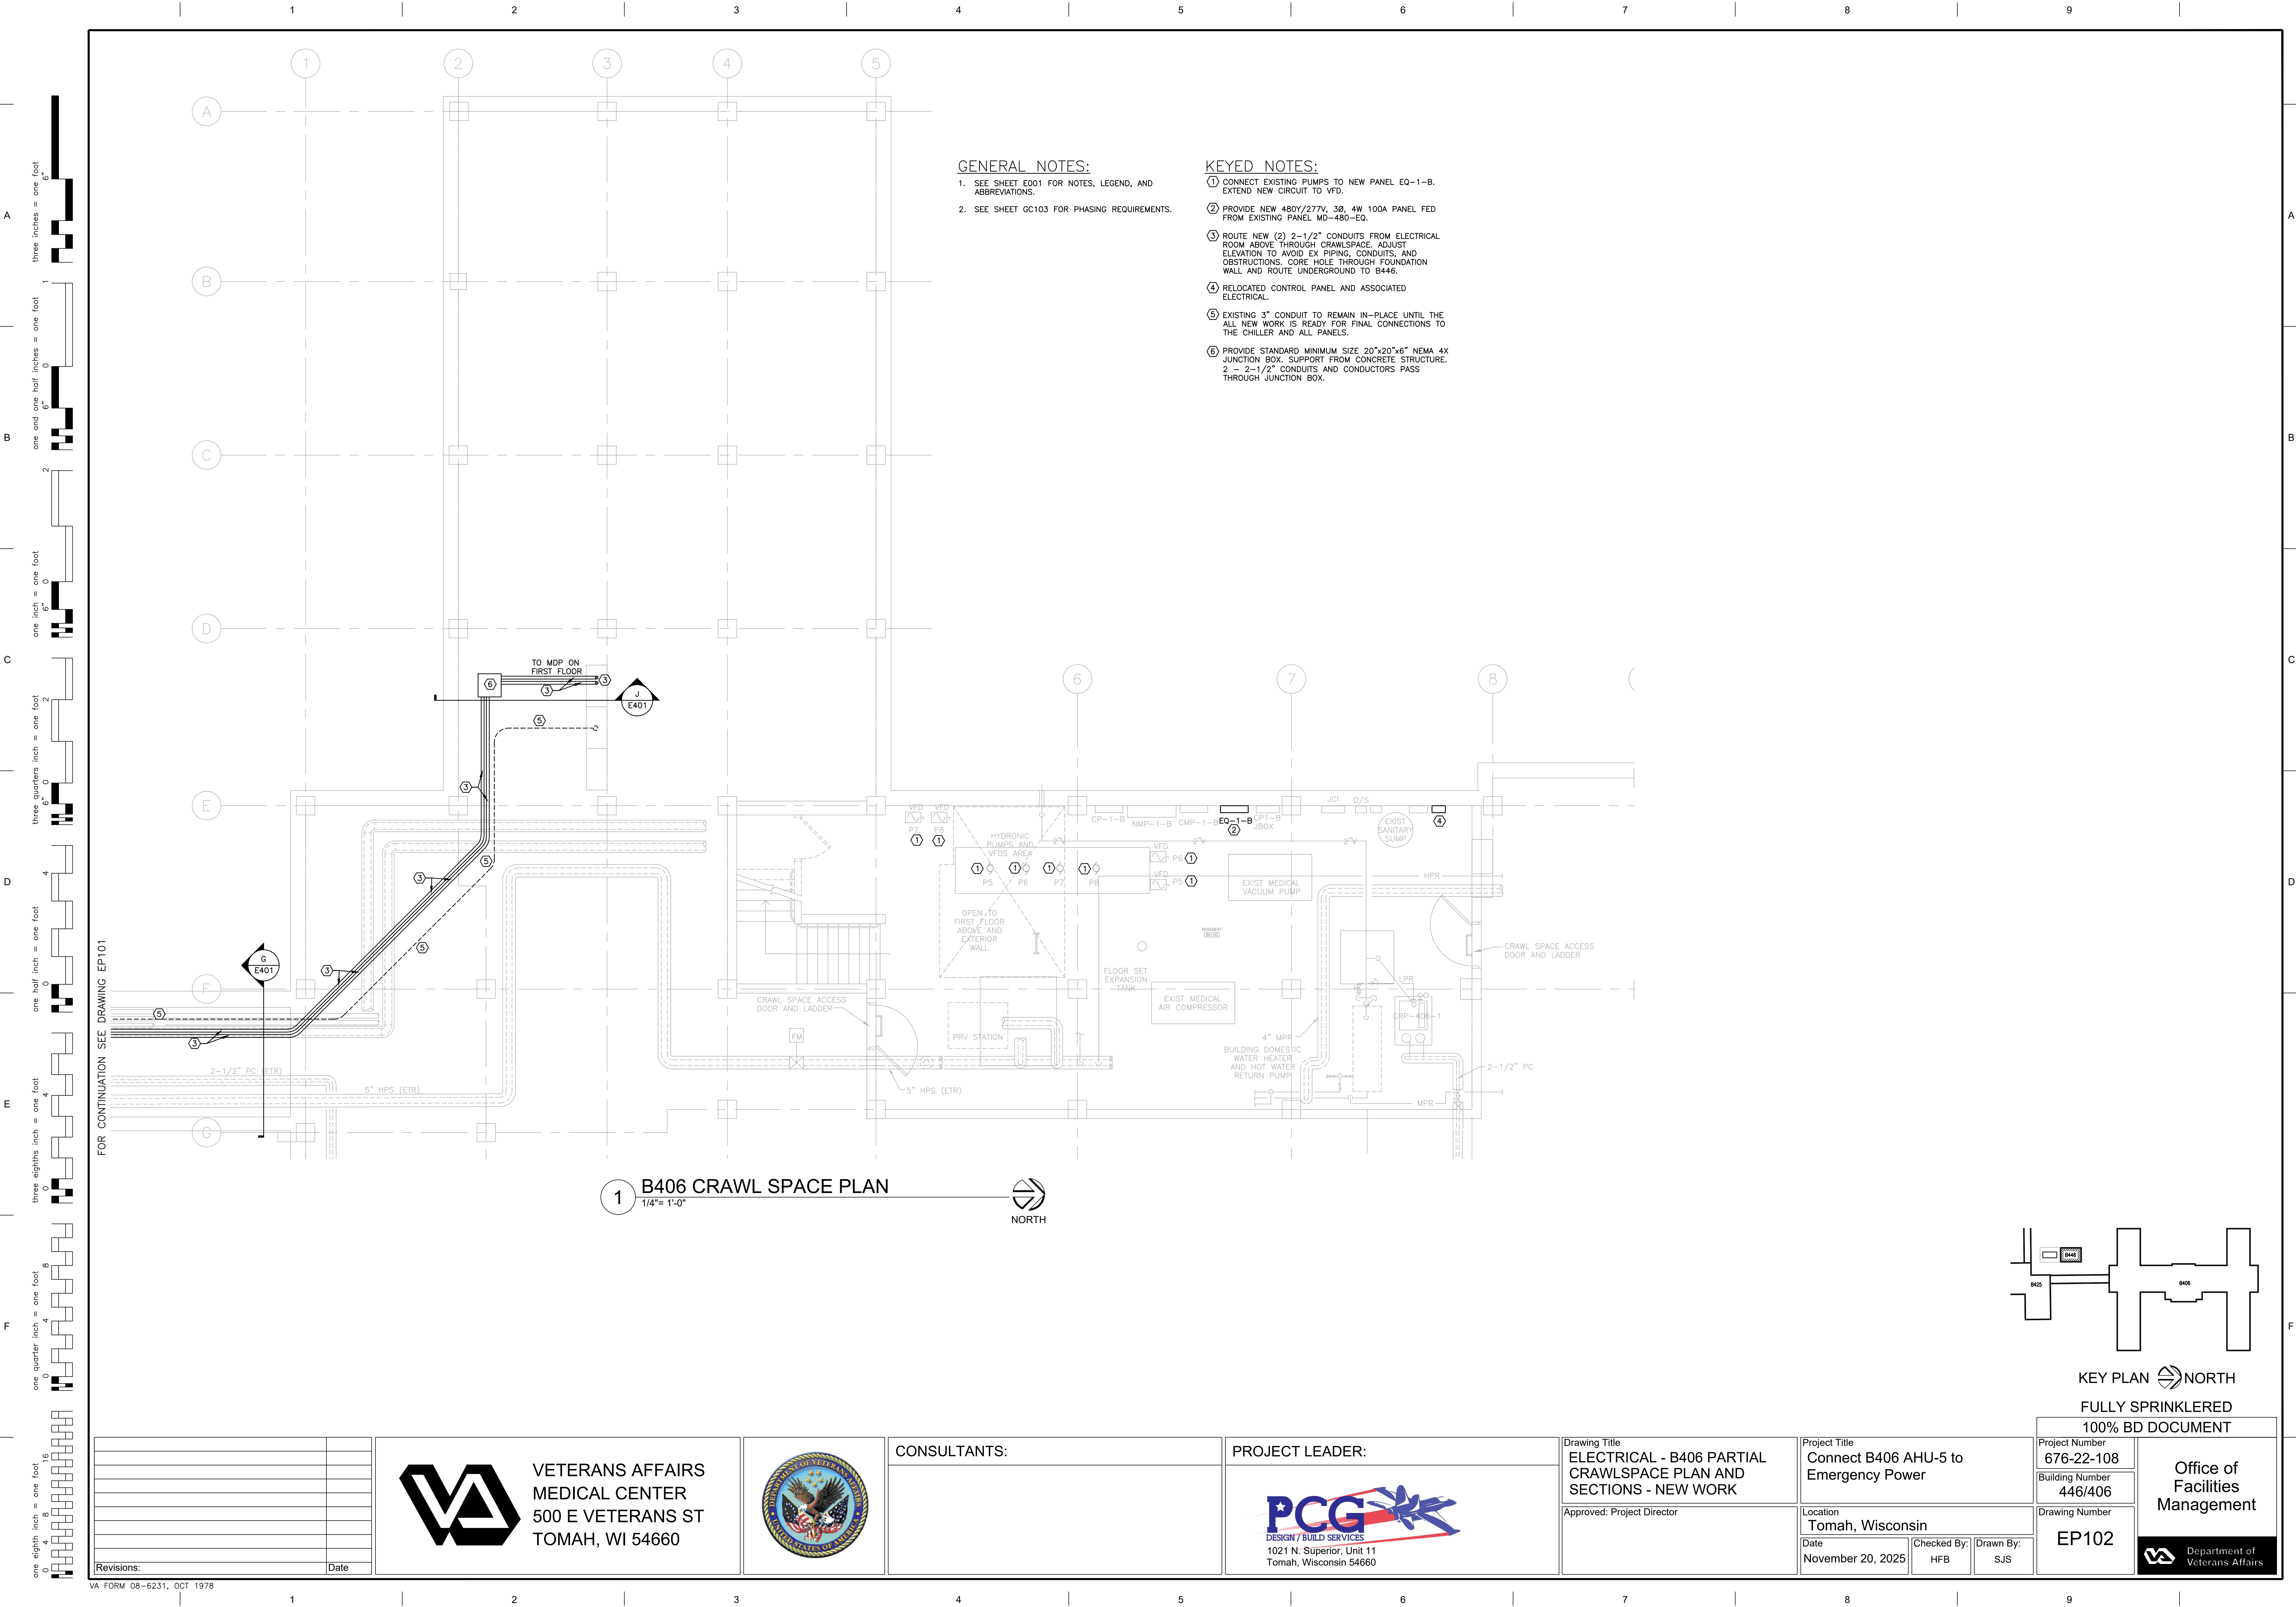

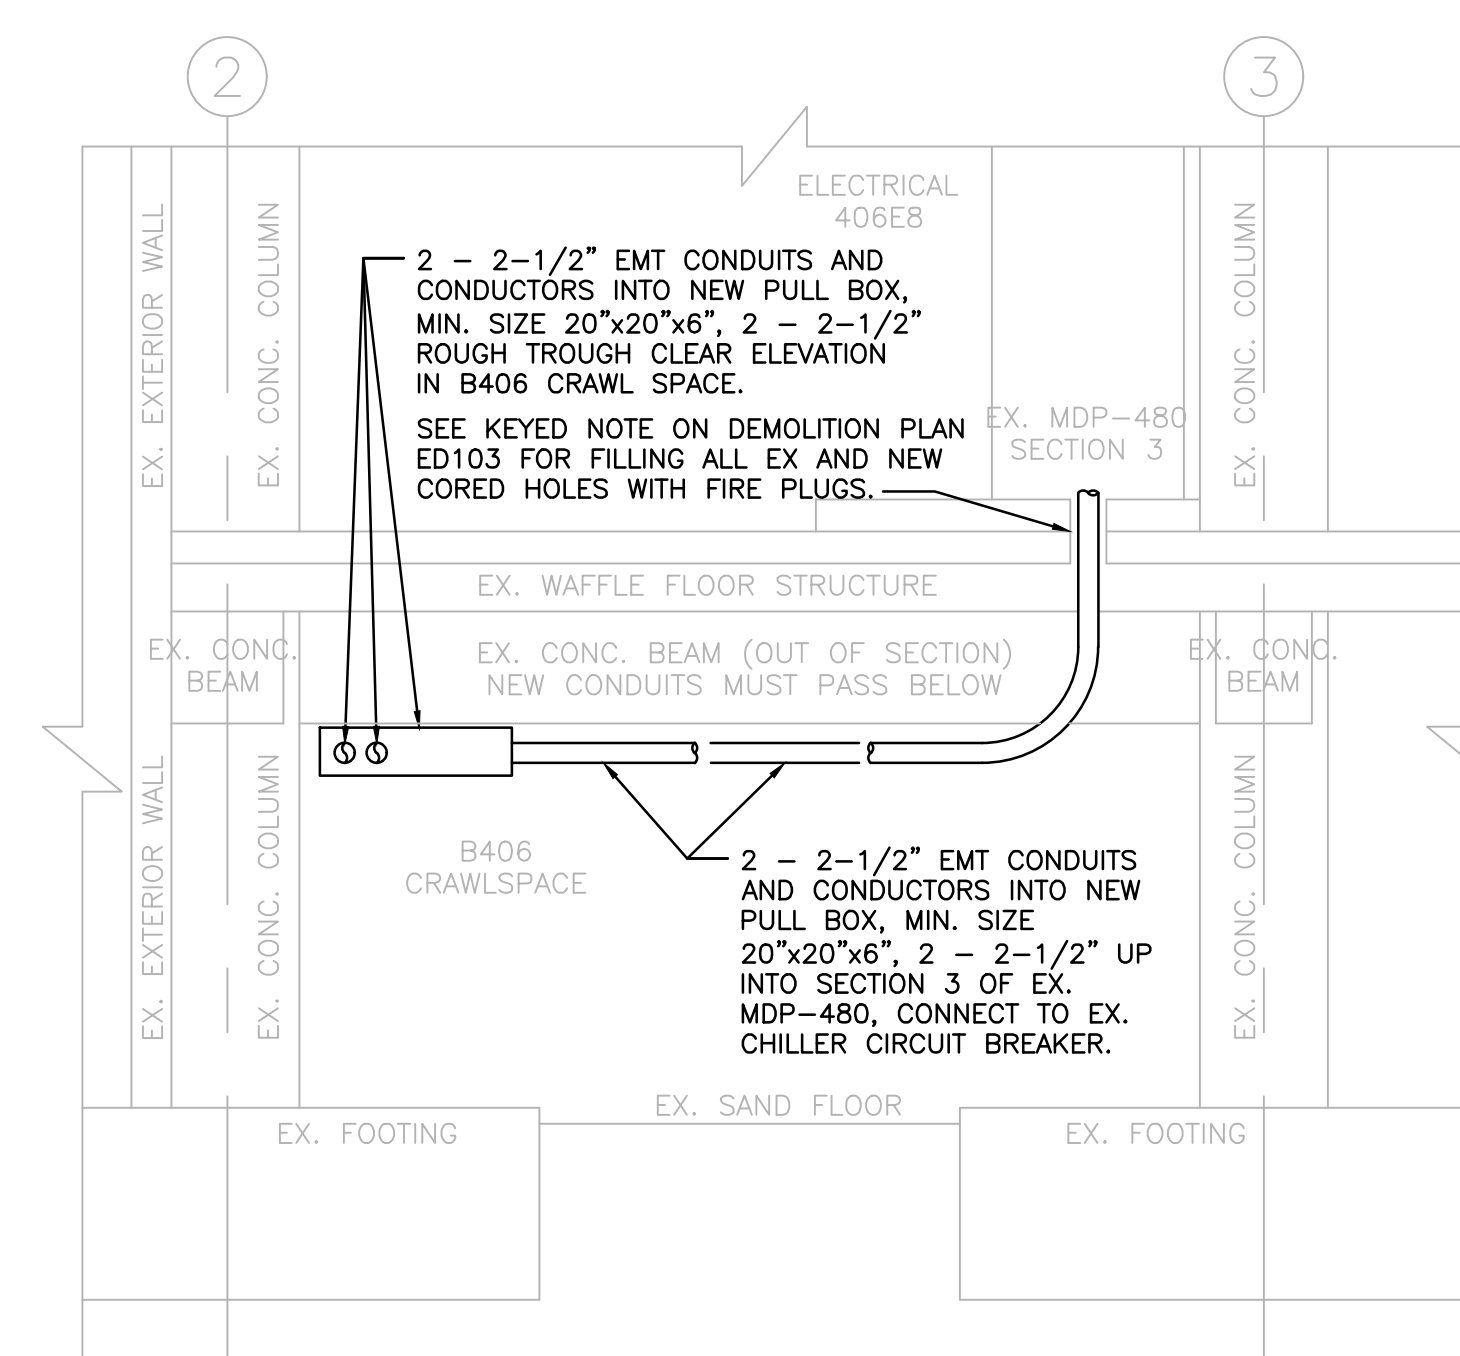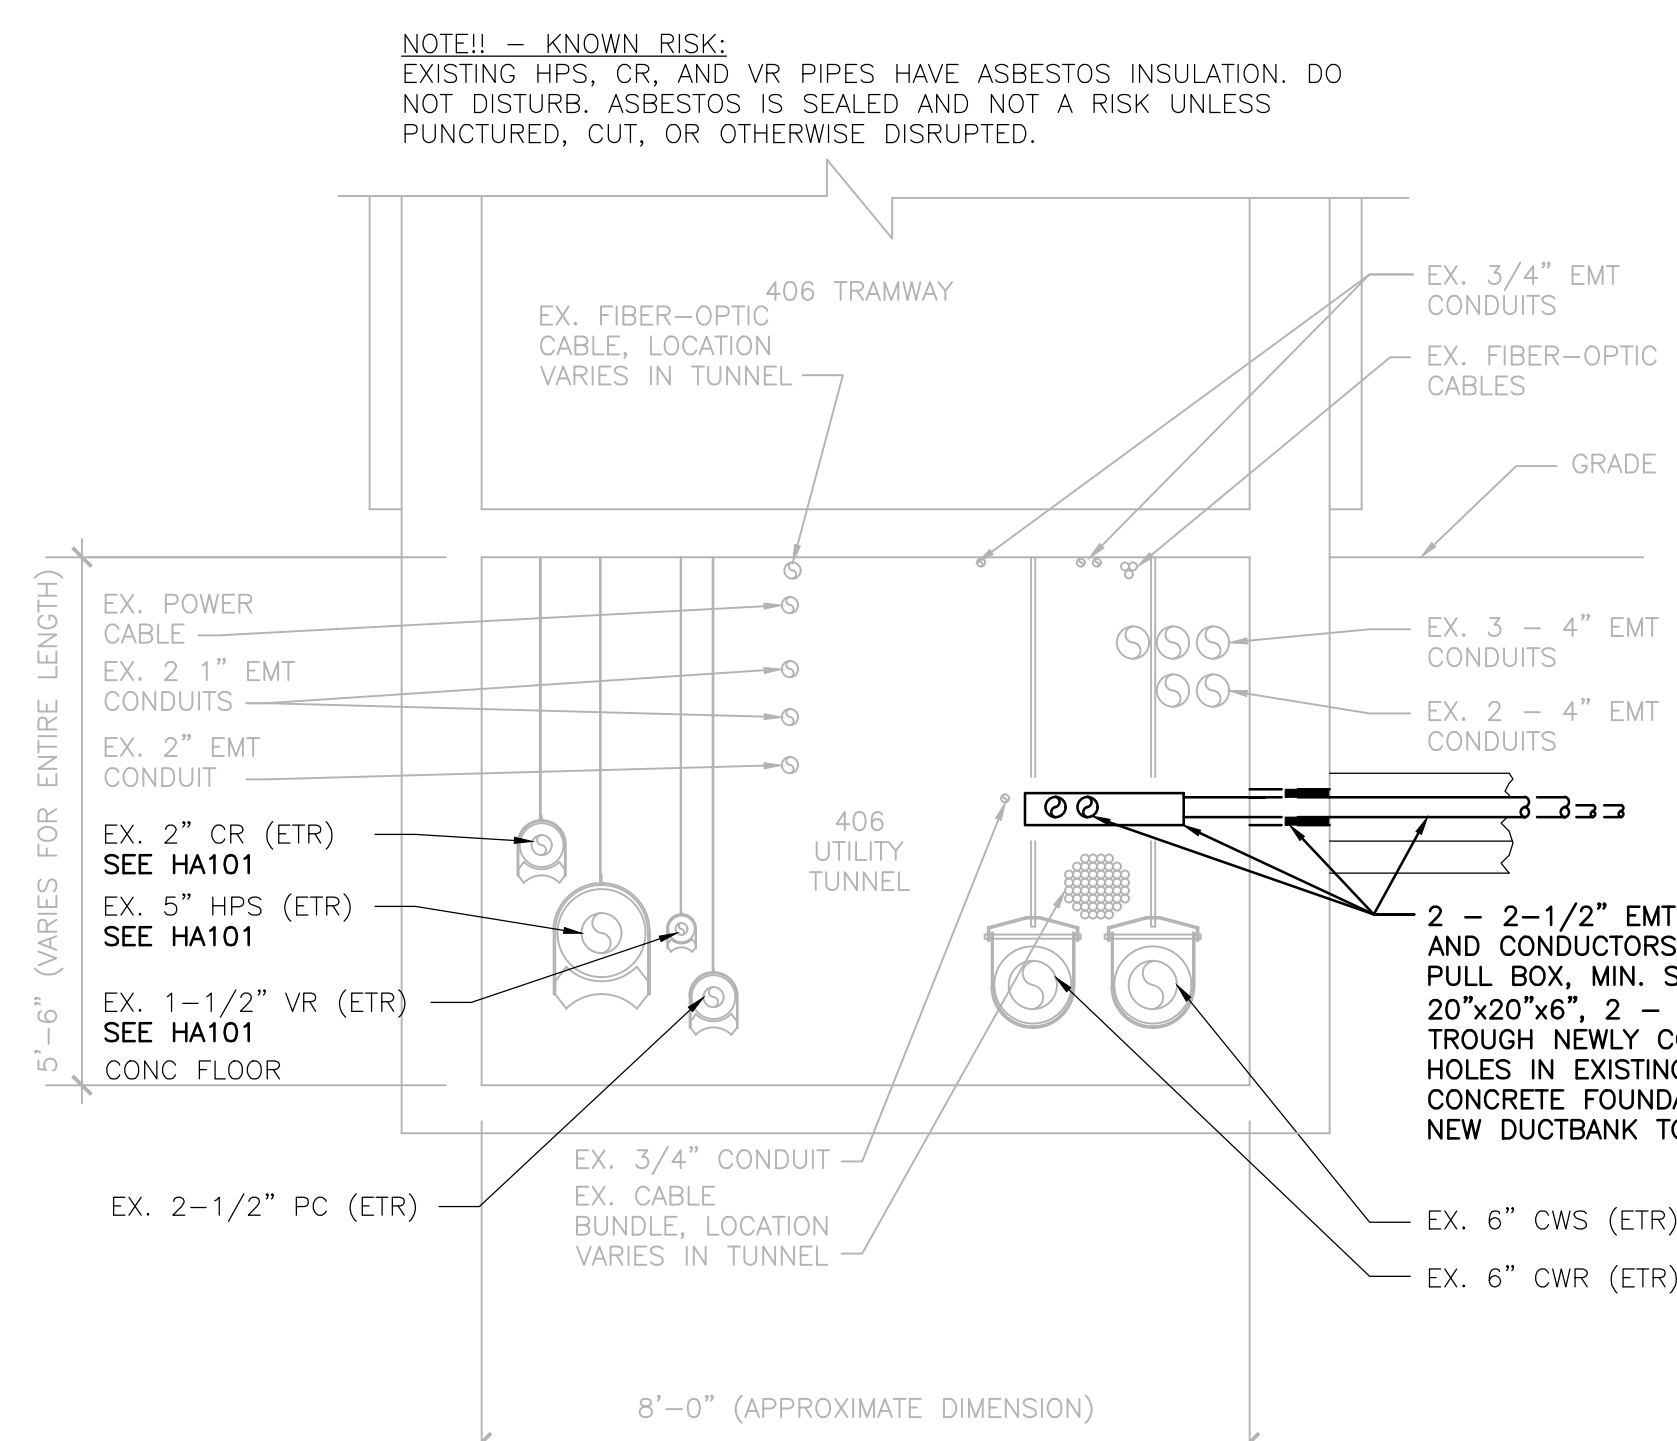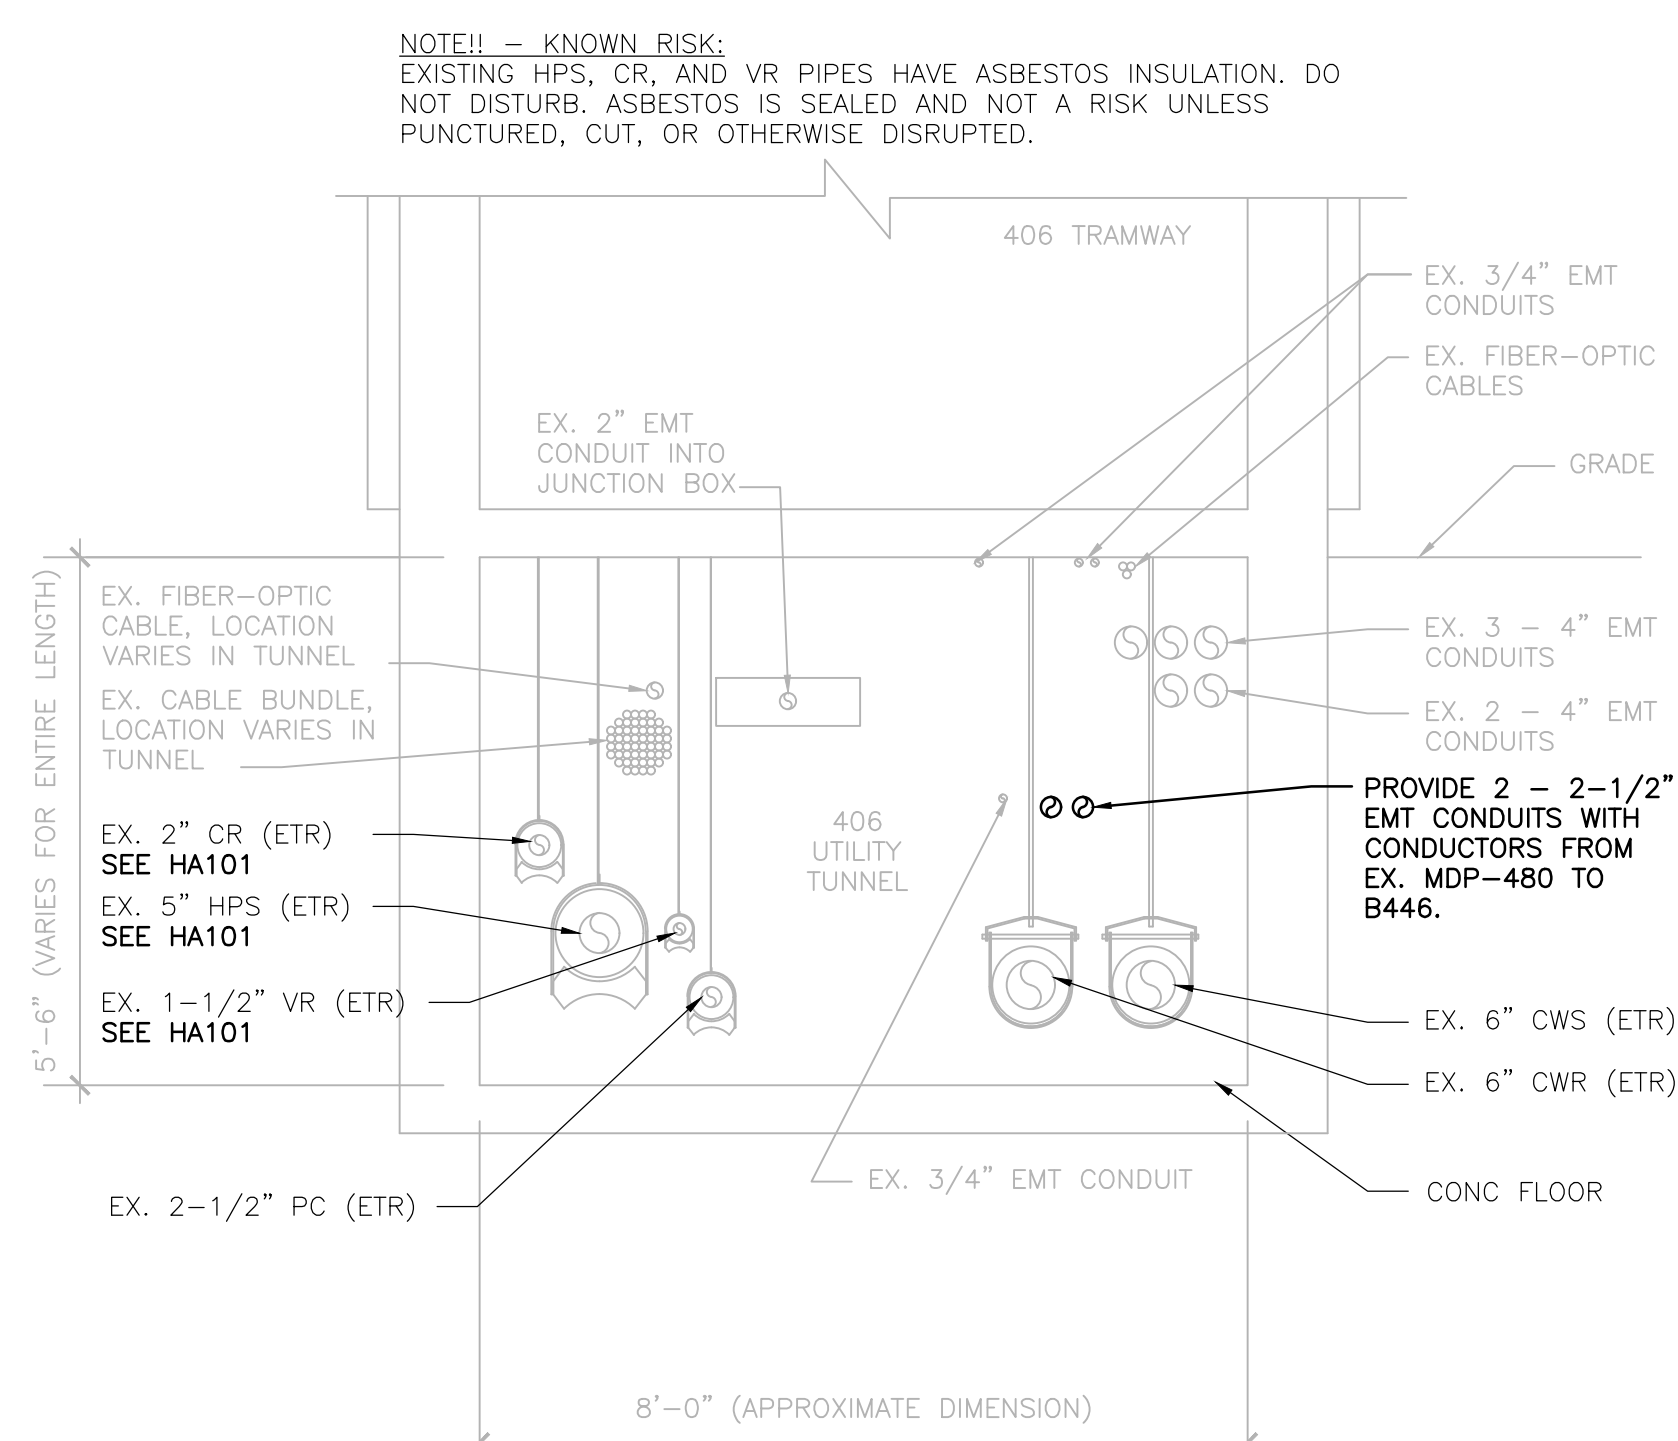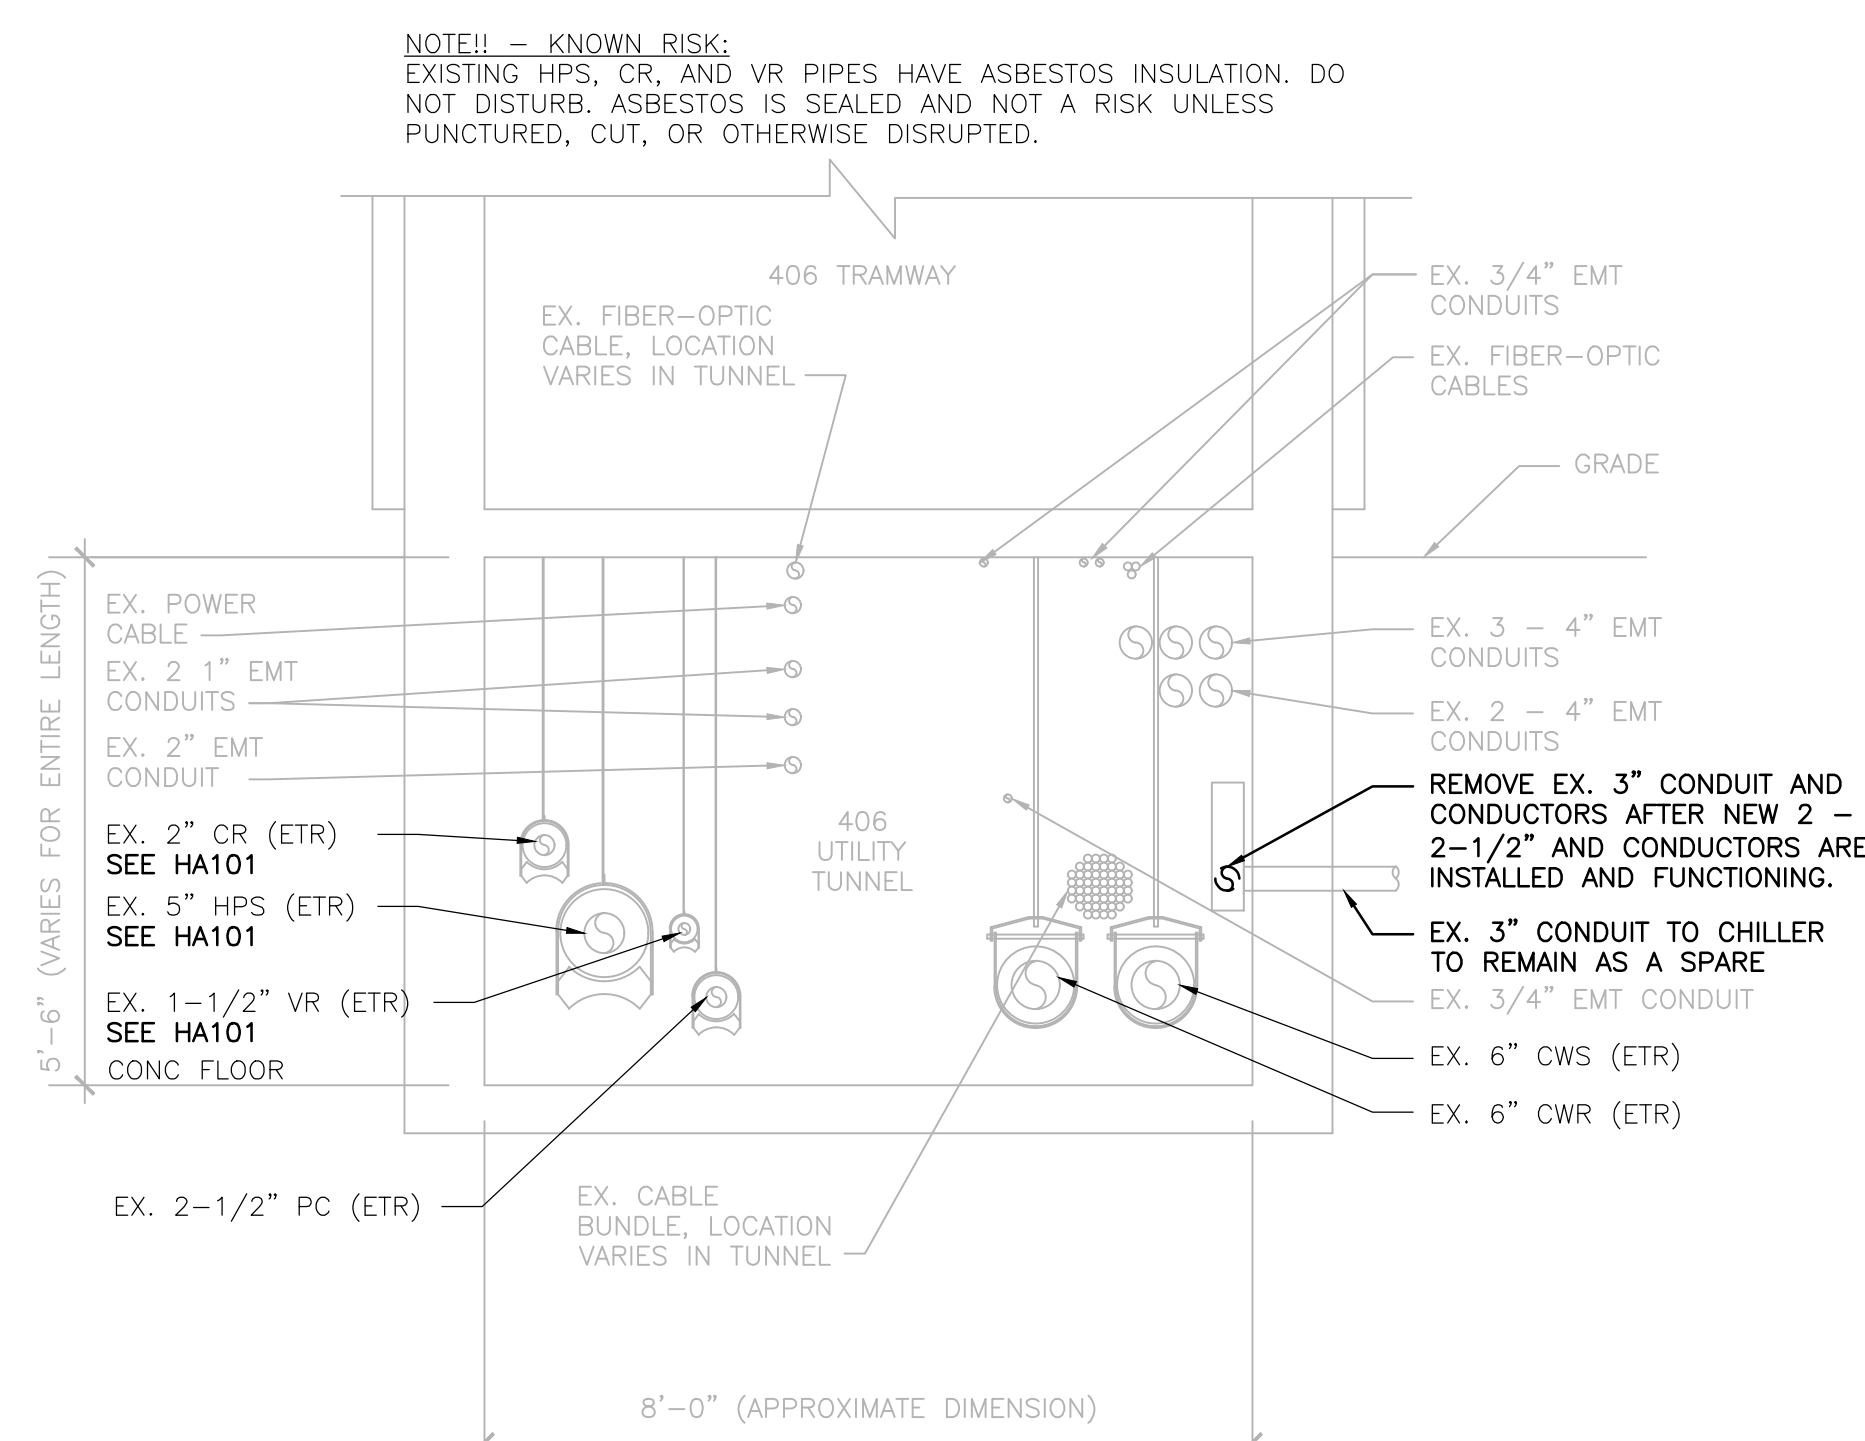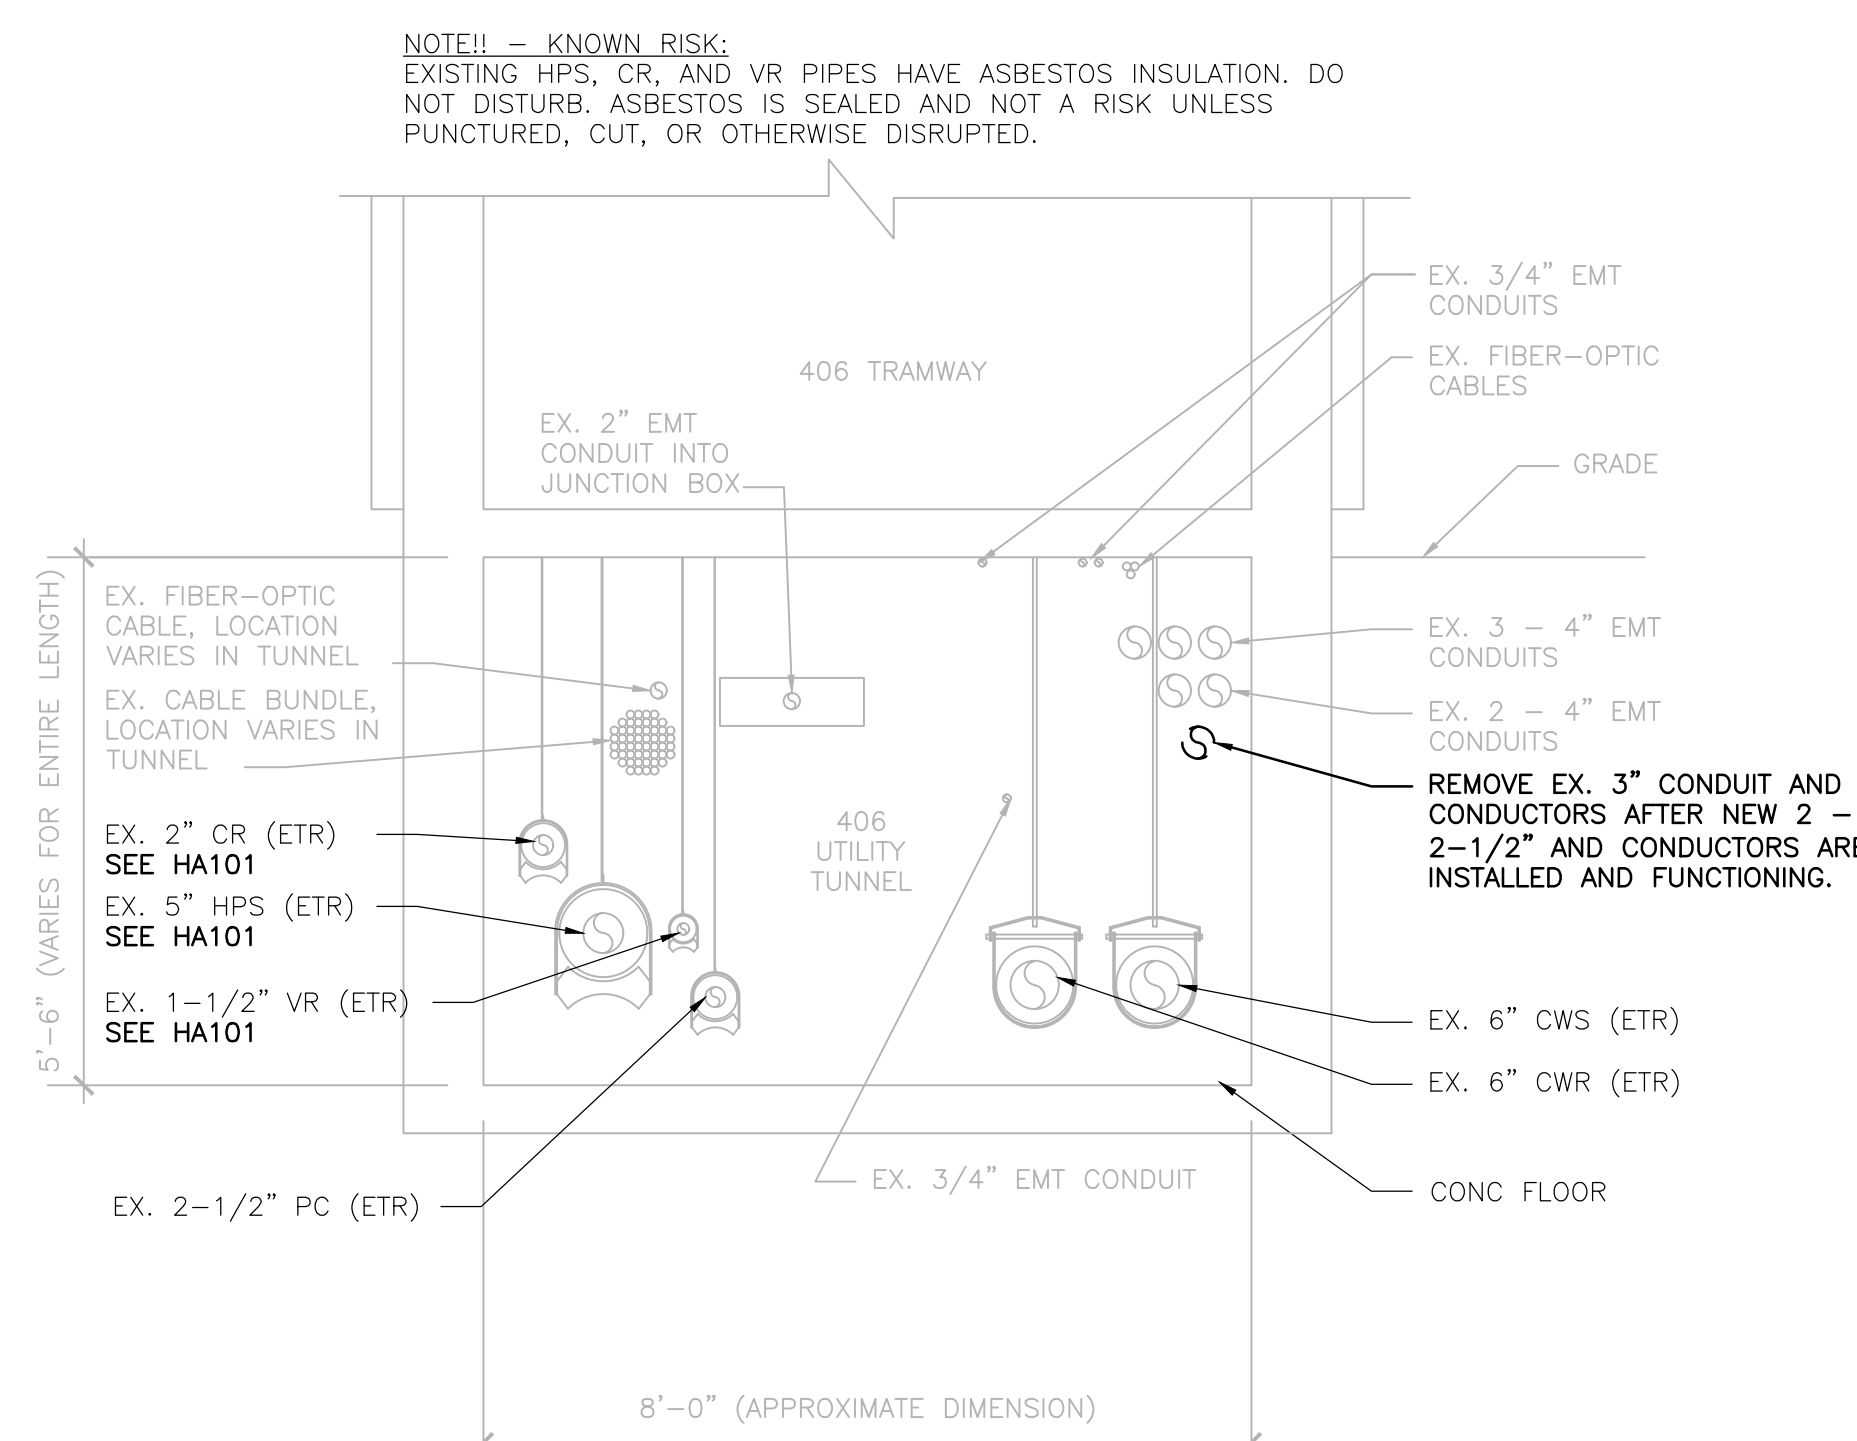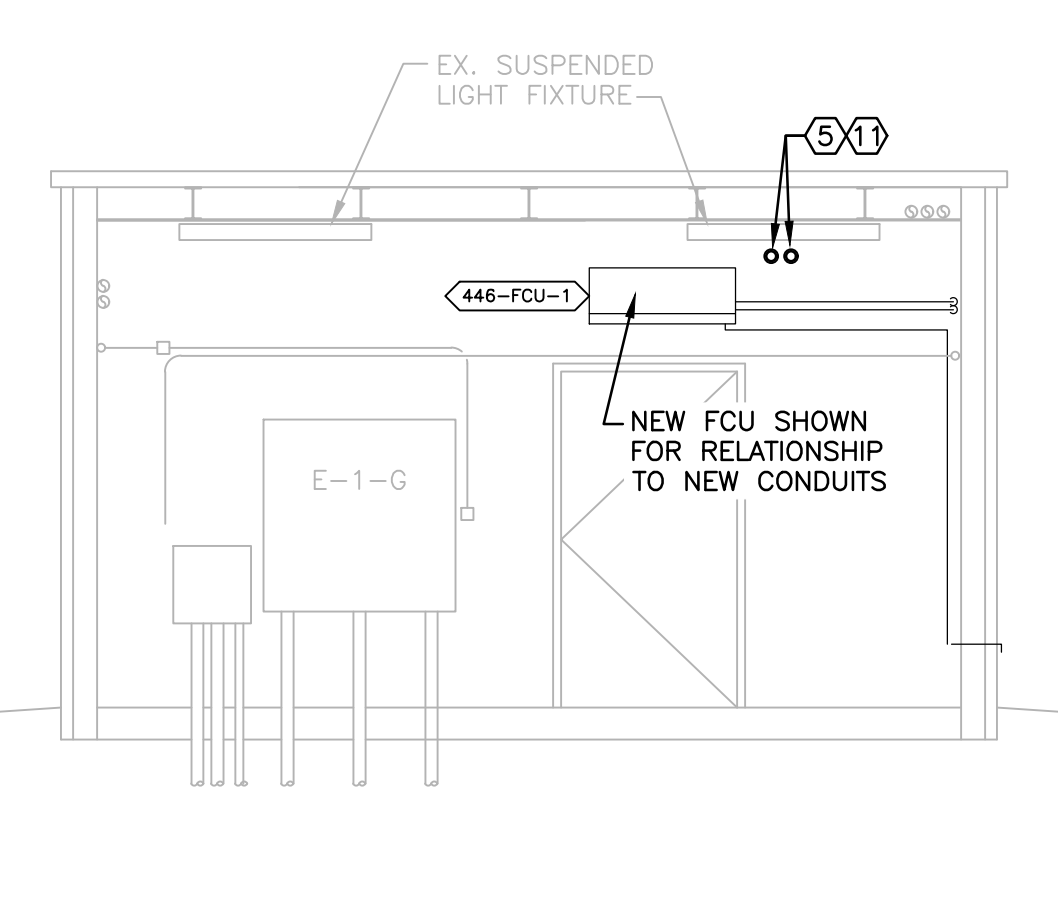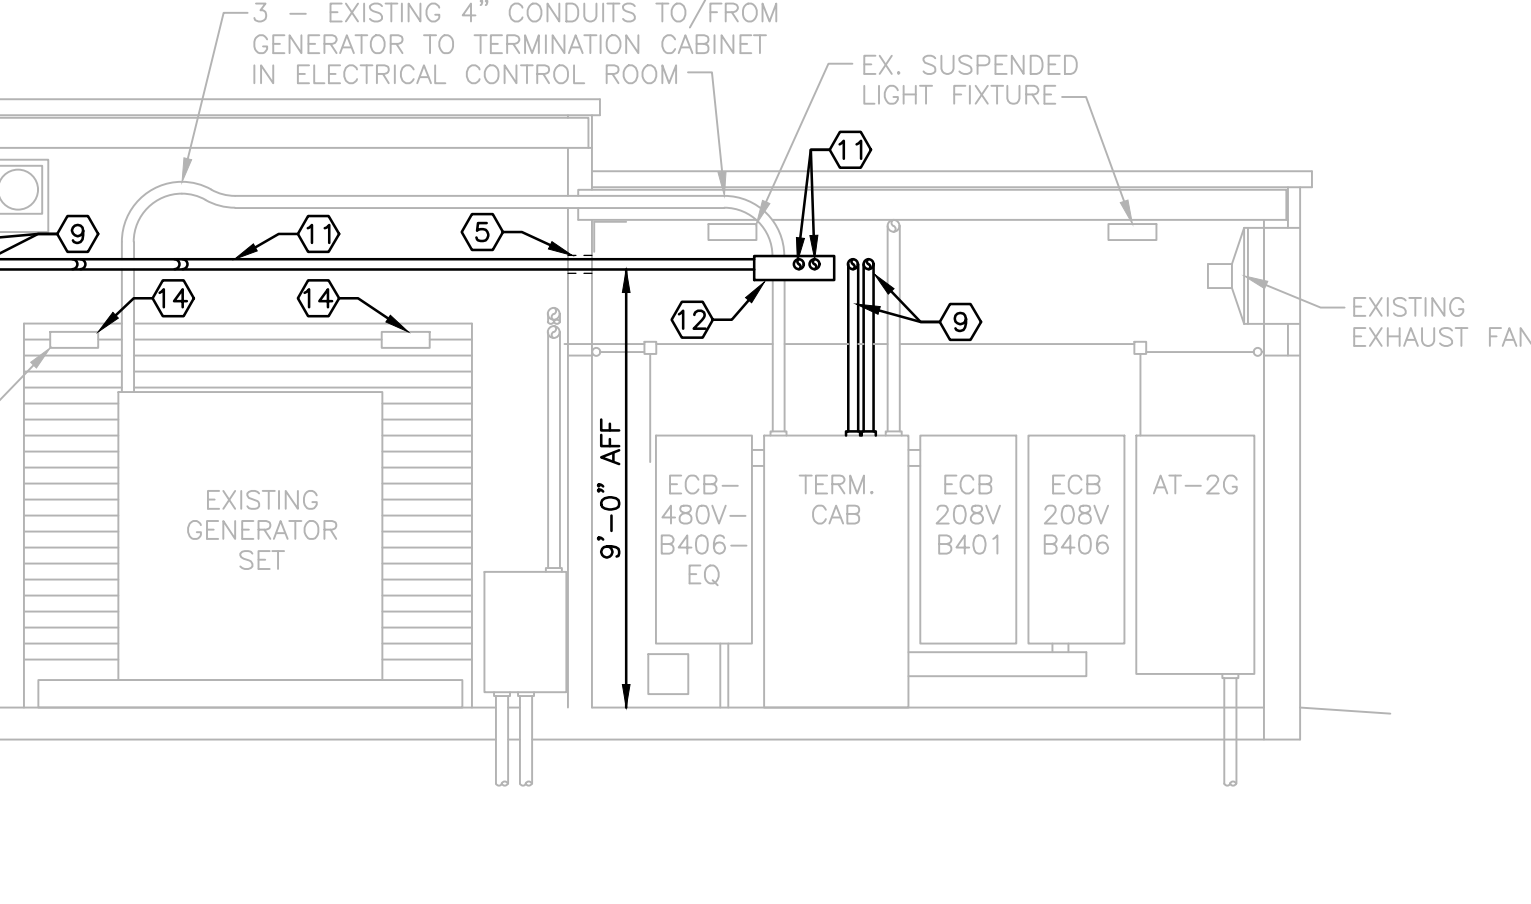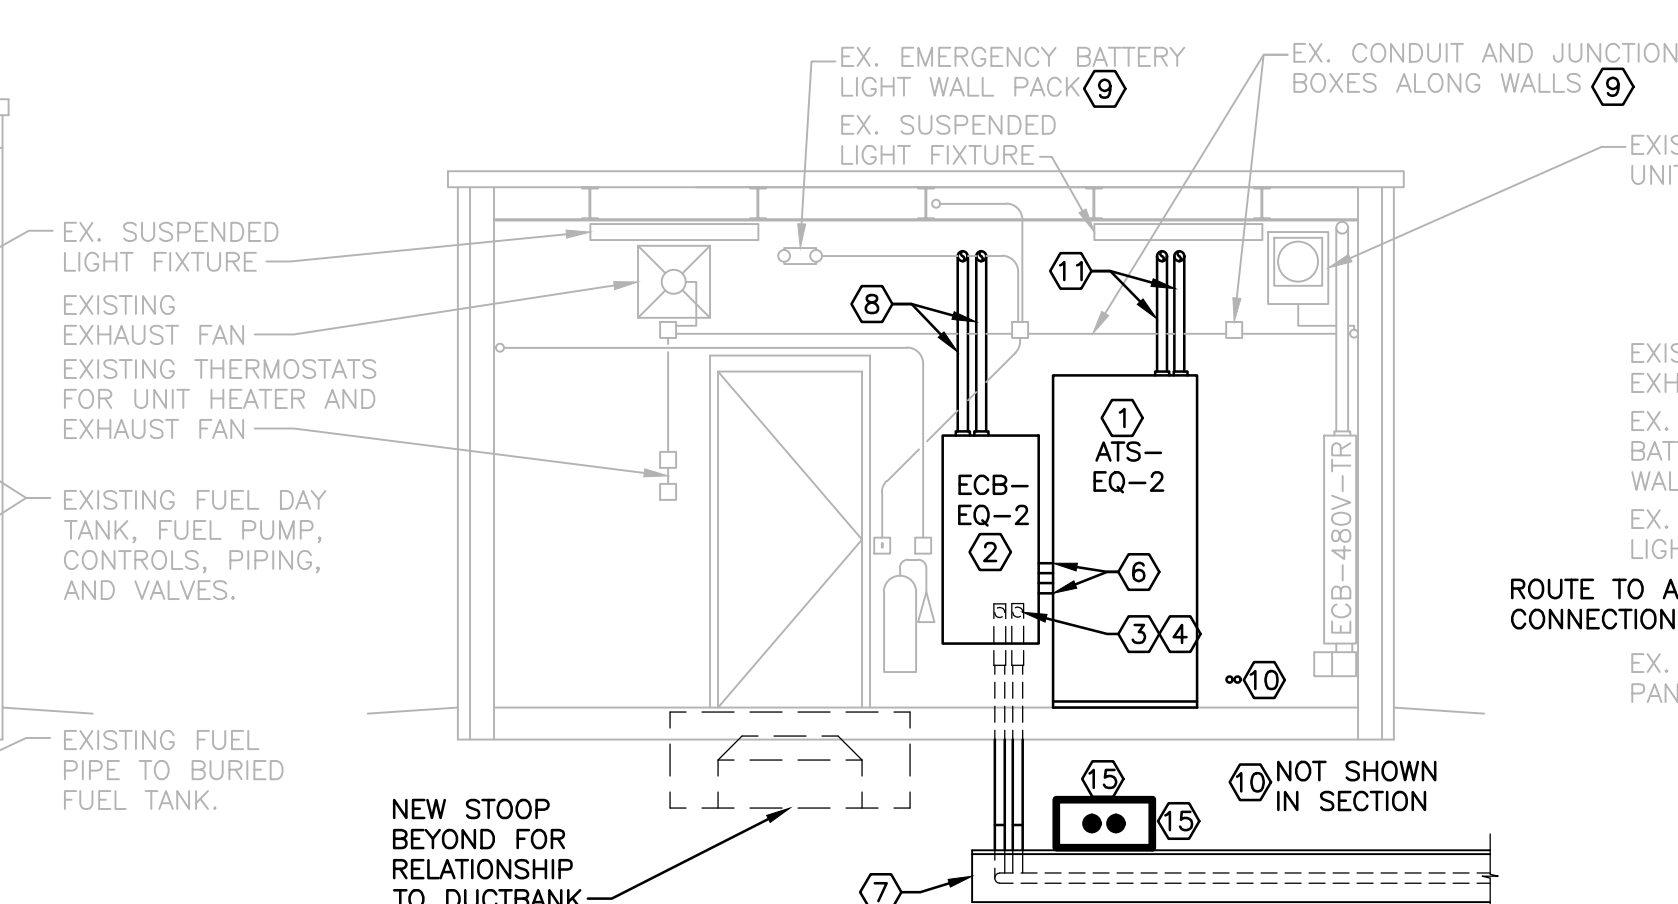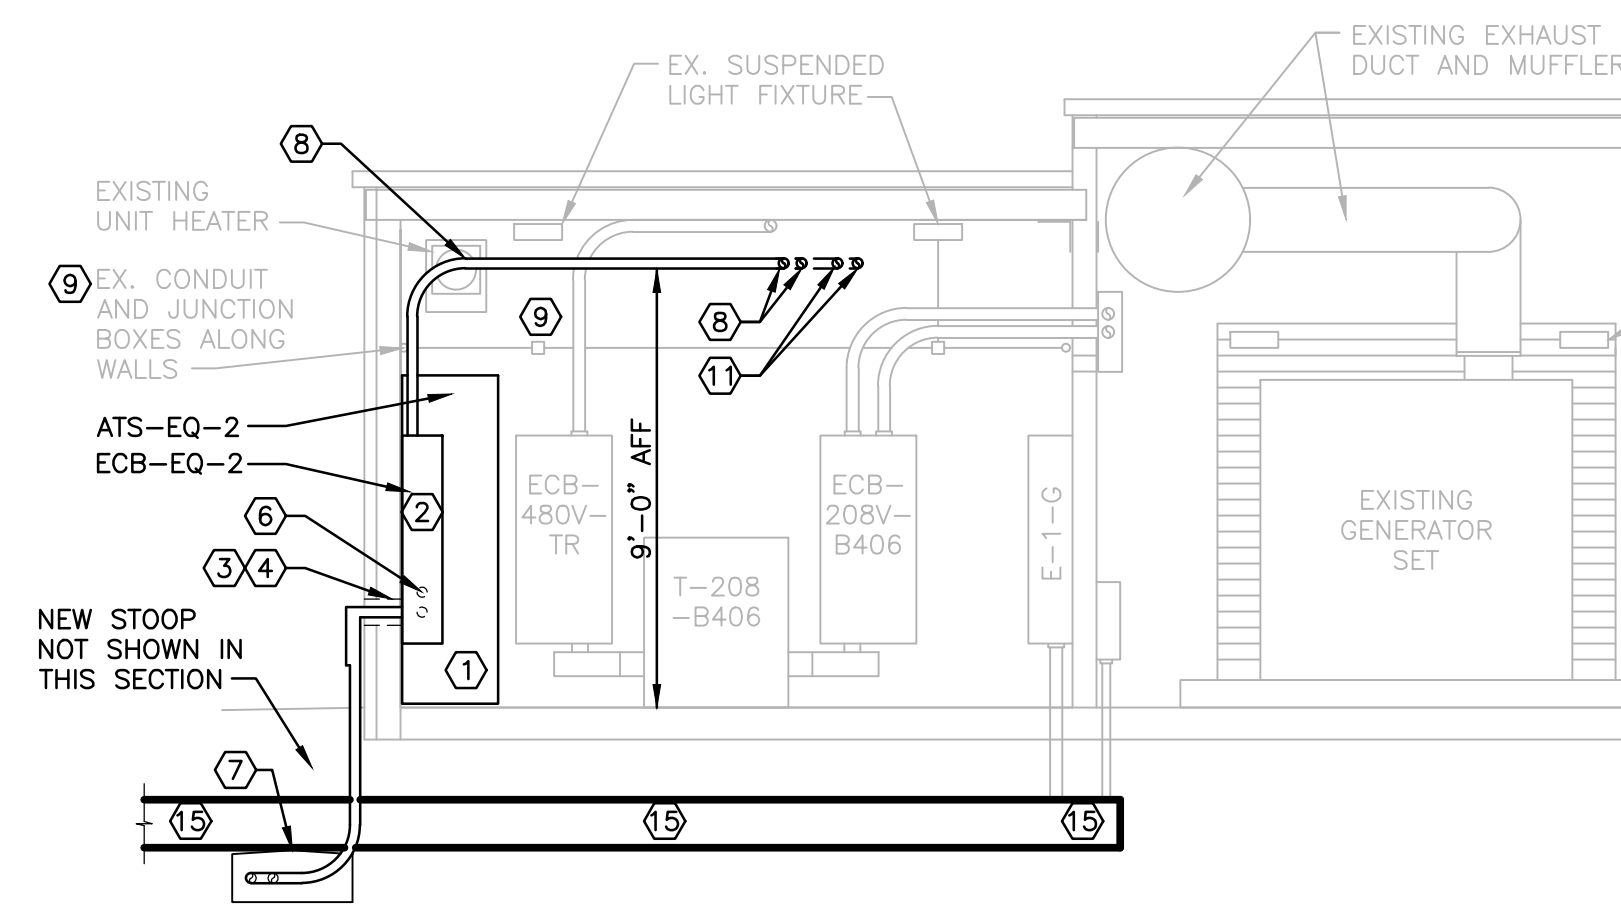

GENERAL PLAN NOTES





1. REFER TO SHEET E001 FOR GENERAL NOTES, SYMBOLS AND ABBREVIATIONS.
2. ELECTRICAL WORK TO BE DONE IN ACCORDANCE WITH PROJECT PHASING. REFER TO SHEETS GC101 THROUGH GC103 FOR MORE INFORMATION.
3. SHUTDOWNS AND SERVICE INTERRUPTIONS SHALL BE COORDINATED WITH COR AND SHALL BE APPROVED IN WRITING BY COR PRIOR TO WORK BEING PERFORMED. A 3 WEEK ADVANCE NOTICE IS REQUIRED FOR ANY PLANT SHUTDOWN.
4. SIZE PULLBOXES AS REQUIRED BY NEC.
5. FIELD VERIFY EXISTING CONDITIONS. COORDINATE WITH CONDUIT RUNS WITH MC.


- ① PROVIDE NEW AUTOMATIC TRANSFER SWITCH (ATS-EQ2). BASIS OF DESIGN CUMMINS MODEL BTPC, 600A.
- ② PROVIDE NEW ENCLOSED CIRCUIT BREAKER AND CONNECT TO EXISTING TERMINATION CABINET.
- ③ PROVIDE 2 - 2-1/2" CONDUITS THROUGH WALL INTO ECB-EQ-2.
- ④ CORE WALL, SEE DETAIL 7 ON E501, FILL ALL-AROUND, BOTH ENDS WITH GROUT.
- ⑤ CORE WALL, SEE DETAIL 6 ON E501.
- ⑥ PROVIDE 2 - 2-1/2" CONDUITS FROM ECB-EQ-2 TO ATS-EQ-2.
- ⑦ SEE DETAILS 2 AND 3 ON E501 FOR DUCTBANK AND CONDUIT REQUIREMENTS.

- ⑤ PROVIDE 2 - 2-1/2" CONDUITS TO/ FROM EGS-EQ- TO TERMINATION CAB. PROVIDE ALL CONDUCTORS AS NOTED ON PLANS AND ONE(LINE)-S. PROVIDE ALL SUPPORTS. PROVIDE ALL EXISTING SUPPORTS. RELOCATED EXISTING SUPPORTS AS NEEDED.
- ⑥ AVOID EXISTING CONDUITS AND JUNCTION BOXES ON WALL. SEE SECTIONS FOR APPROXIMATE LOCATIONS.
- ⑦ PROVIDE 2 - 1-1/2" SPARE CONDUITS THROUGH WALL AND CAP 3" INTO ELECTRICAL ROOM, PROVIDE STEEL SIGN STATING "SPARE EMPLY CONDUITS DOWN TO 2" BANK ROUTED TO 8406 UTILITY TRAMWAY CAP 3" BOTH ENDS.
- ⑧ PROVIDE 2 - 2-1/2" CONDUITS TO/ FROM ATS-EQ- TO EXISTING CHILLER (ACCH-1). PROVIDE ALL CONDUCTORS AS NOTED ON PLANS AND ONE(LINE)-S. PROVIDE ALL SUPPORTS. AVOID EXISTING SUPPORTS. RELOCATED EXISTING SUPPORTS AS NEEDED.

- ⑦ PROVIDE 20"x20"x4" PULL BOX WITH KNOCKOUT PLUGS, SEE SPECIFICATIONS, SUPPORT BOX TO STRUCTURE, AVOID EXISTING SUPPORTS, ADJUST EXISTING SUPPORTS AS NEEDED.
- ⑧ PROVIDE 20"x20"x4" PULL BOX WITH KNOCKOUT PLUGS, SEE SPECIFICATIONS, SUPPORT BOX TO STRUCTURE, THIS PULL-BOX MUST BE WEATHERPROOF NEMA 4X
- ⑨ MOVE AND REINSTATE CONDUIT AND SUPPORTS FOR EXISTING LIGHT FIXTURE.
- ⑩ PROBABLE LOCATION OF EXISTING CONDUITS/DUCTBANK. LOCATION PROVIDED BY UNDERGROUND MAPPING SERVICE. HAND DIG OR POT-HOLE EXCAVATION FOR NEW DUCTBANK IN THIS CASE. SEE DRAWING FOR EXISTING AND ADDITIONAL COORDINATION. EXACT DEPTH AND QUANTITIES NOT KNOWN. COORDINATE AND FOLLOW KEYED NOTE #9 ON C101 ALONG WITH GENERAL CONTRACTOR AND SITE WORK CONTRACTOR.

-

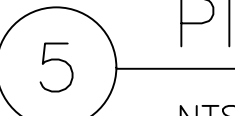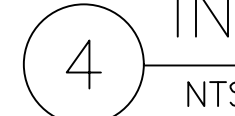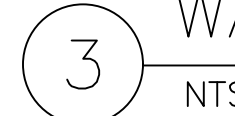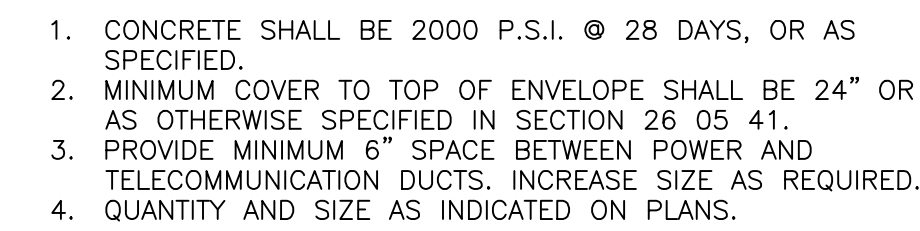VA FORM 08-6231, OCT 1978

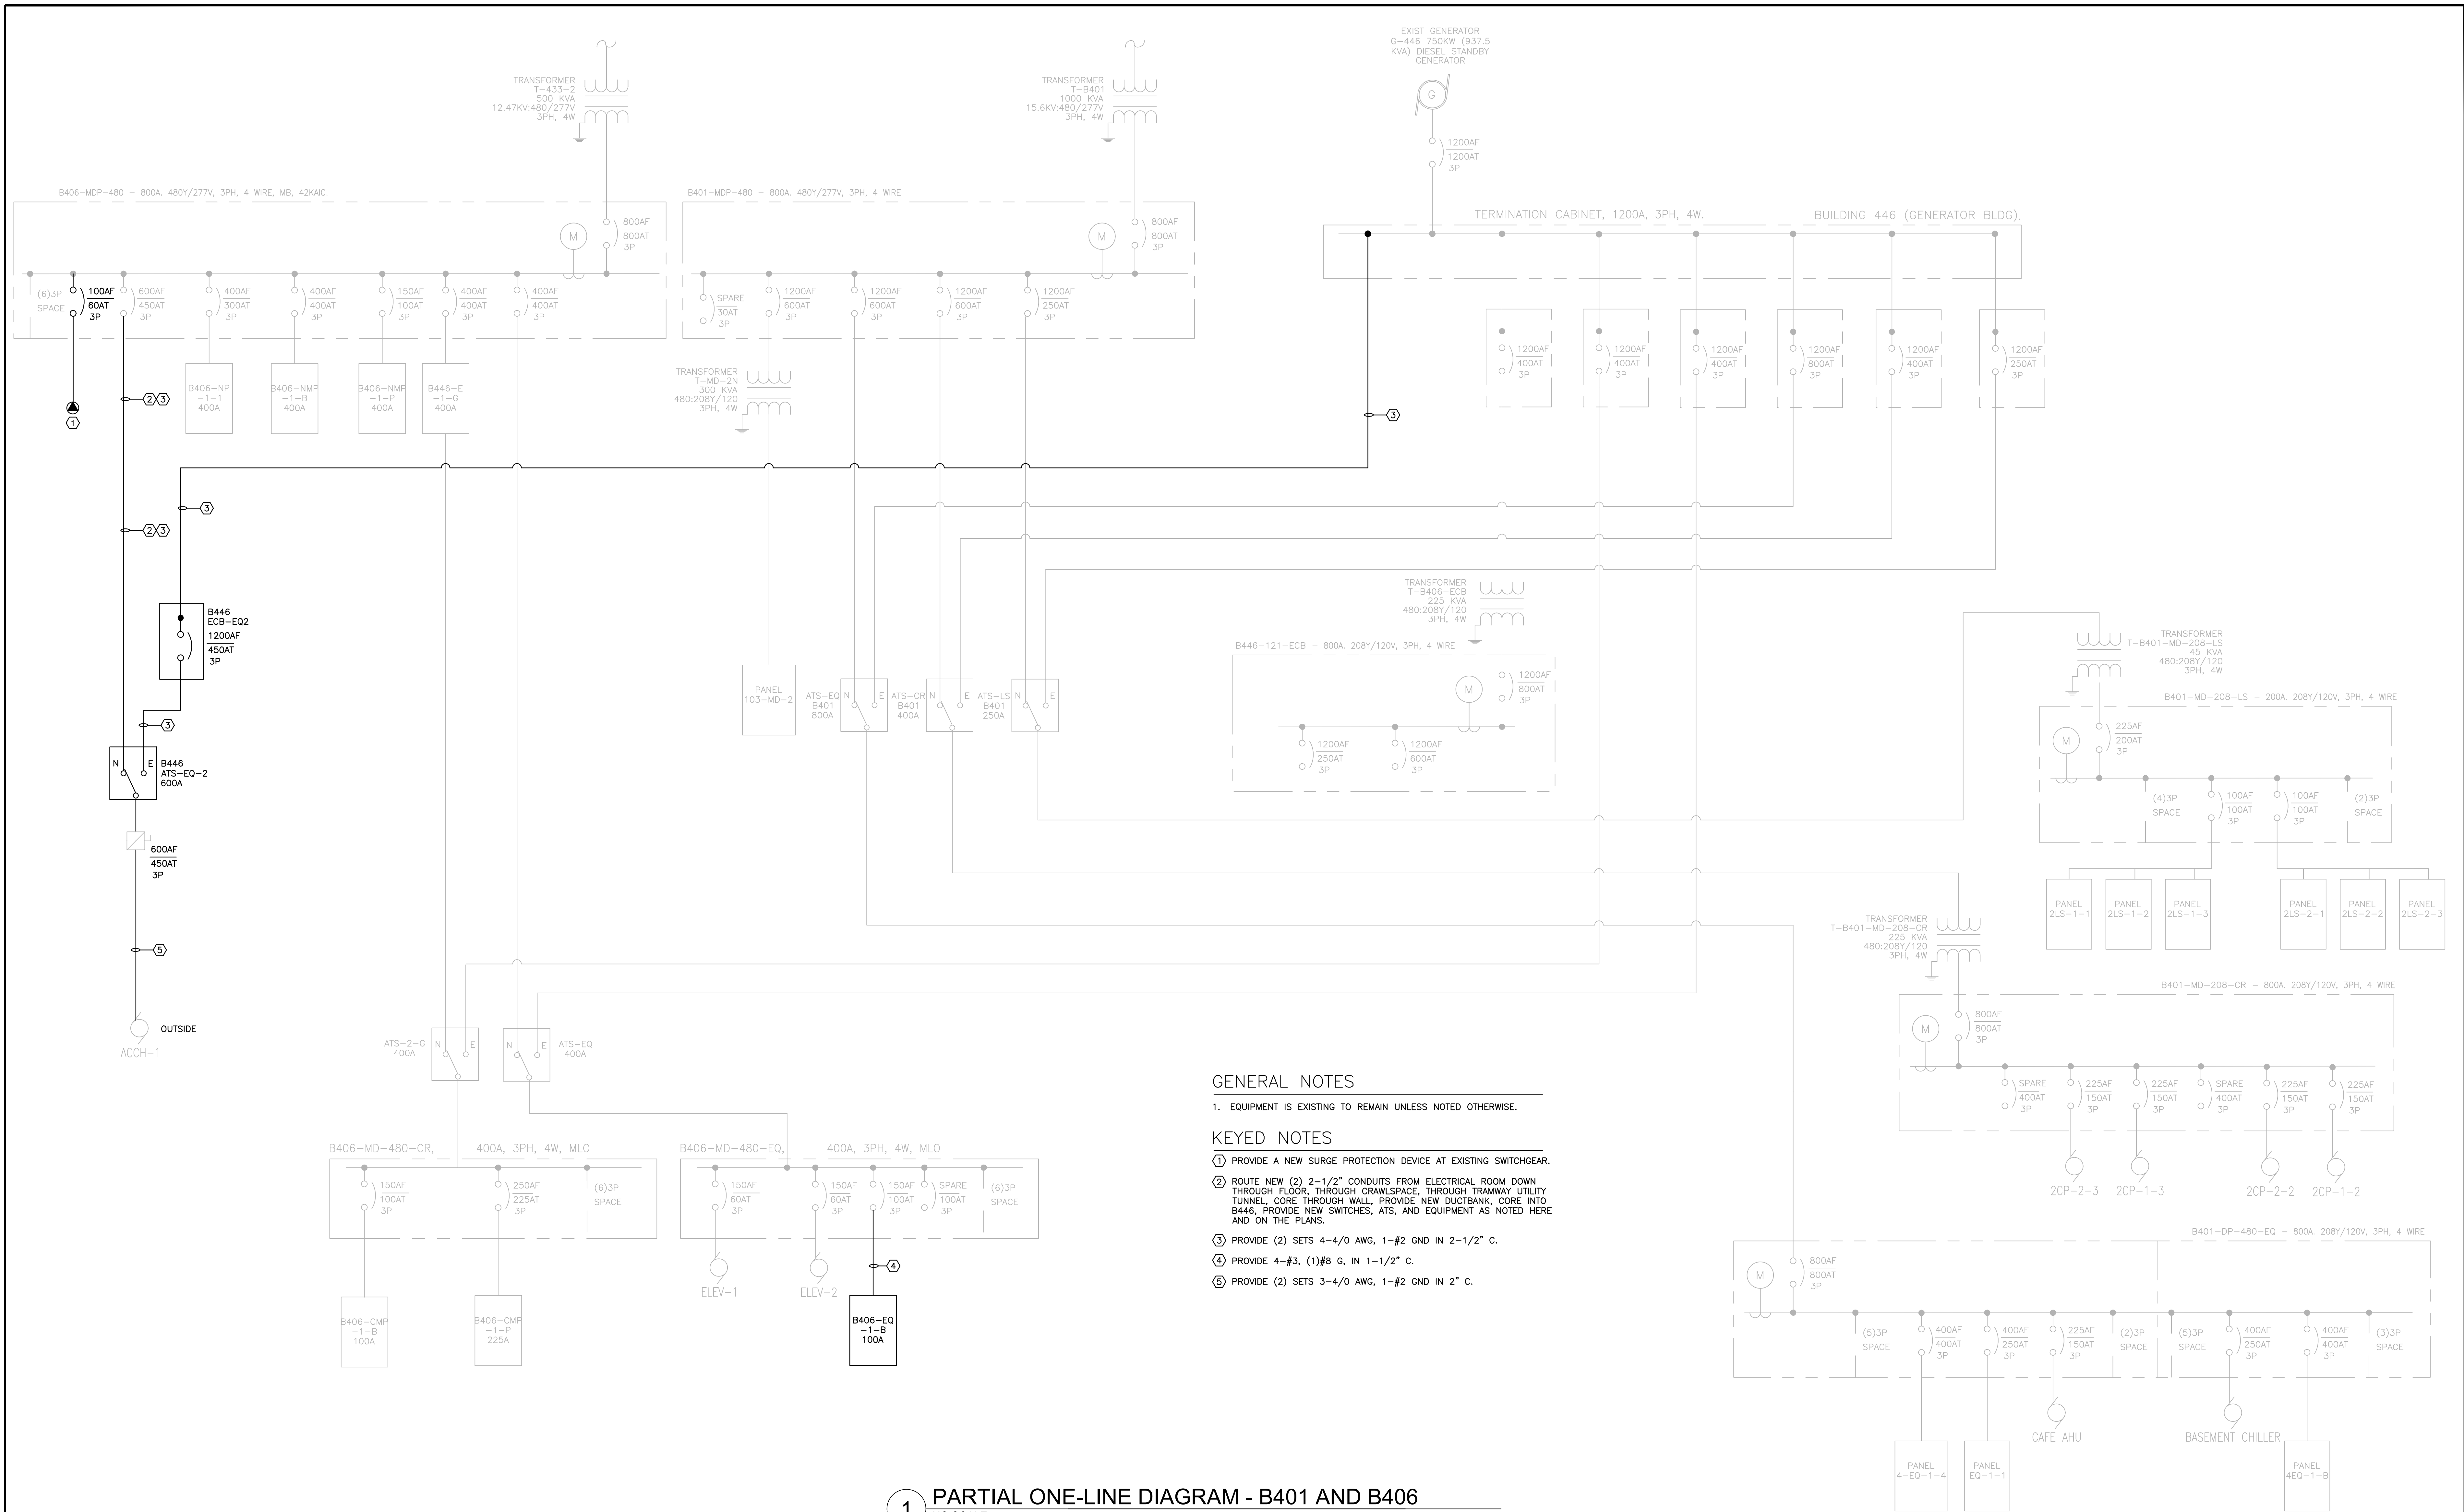[illegible]

PANEL B406-480-EQ-1-B -- 480Y/277V 3PH 4W 100A											
CCT. NO.	BRKR.	DESCRIPTION	PHASE LOADING (KVA)						DESCRIPTION	BRKR.	CCT. NO.
			A		B		C				
1		PUMP VFD P8	5.15	5.15					PUMP VFD P7	45/3	2
3	45/3				5.15	5.15					4
5							5.15	5.15			6
7		PUMP VFD P6	3.38	3.38					PUMP VFD P5	35/3	8
9	35/3				3.38	3.38					10
11							3.38	3.38			12
13		SPARE							SPARE	30/3	14
15	20/3										16
17											18
19		SPARE							SPACE		20
21	20/3										22
23											24
25		SPACE							SPACE		26
27											28
29											30

RATING			CALCULATED LOAD WITH NEC DEMAND FACTORS		
<u>100</u> A, 480Y/277 V, 3 PH, 4 W MAIN LUGS MIN. AIC RATING <u>14,000</u> A			CONTINUOUS LOAD X 125% <u>0.00</u> KVA NON-CONTINUOUS LOAD <u>51.18</u> KVA EXISTING LOAD X 125% <u>0.00</u> KVA RECEPTACLE LOAD, ≤ 10 KVA <u>0.00</u> KVA RECEPTACLE LOAD > 10KVA @ 50% <u>0.00</u> KVA KITCHEN LOAD @ <u>100%</u> <u>0.00</u> KVA PLUS 25% OF LARGEST MOTOR <u>0.00</u> KVA TOTAL KVA <u>51.18</u> KVA TOTAL A <u>62</u> A AT 480V, 3PH		

NOTES: