

U.S. DEPARTMENT OF VETERANS AFFAIRS
VA PALO ALTO HEALTHCARE SYSTEM
3801 MIRANDA AVENUE
PALO ALTO, CA 94304

RENOVATION AND EXPANSION OF SPS/ SCS

FF&E PLAN PHASE 1
VA PROJECT NUMBER: 640-23-108



Office of
Facility
Planning and
Development
VA

Project Title
VA Palo Alto - SPS/ SCS Renovation

City of Palo Alto
Santa Clara County, CA
Building Number
100
Project Number:
640-23-108

SHEET NOTES

FF&E PLAN
PHASE I

Revision:	Issue Date
END-USERS SIGN-OFF	05/09/2025

Drawing Title:
Title Sheet

Reference To:

Scale: SEE DWG.	Drawing Number: VA-000
Date: 05/09/25	

City of Palo Alto
Santa Clara County, CA
Building Number
100
Project Number:
640-23-108

FF&E PLAN
PHASE I[illegible]

Drawing Title:
Overall Existing B-100 Basement
Floor Plan

Reference To

Scale:
SEE DWG.
Date:
05/09/25

Drawing Number

VA-001

SHEET NOTES:

① EXISTING SCS STORAGE SPACES TO REMAIN

COPYRIGHT © BY HOEFER WYSOCKI ARCHITECTS, LLC

11/27/2024 9:39:57 AM

VA FORM 08-623

GSF = 78,527 SQ.FT
NSF = 71,183 SQ.FT

City of Palo Alto
Santa Clara County, CA
Building Number
100
Project Number:
640-23-108

FF&E PLAN
PHASE I[illegible]

Drawing Title:
Overall New B-100 Basement Floor
Plan

Reference To

Scale:
SEE DWG.

Date:
05/09/25

Drawing Number

VA-003

SHEET NOTES:

① EXISTING SCS STORAGE SPACES TO REMAIN


COPYRIGHT © BY HOEFER WYSOCKI ARCHITECTS, LLC

11/27/2024 9:39:57 AM

VA FORM 08-623

1 OVERALL NEW B-100 BASEMENT FLOOR PLAN
NTS

GSF = 78,527 SQ.FT
NSF = 71,183 SQ.FT

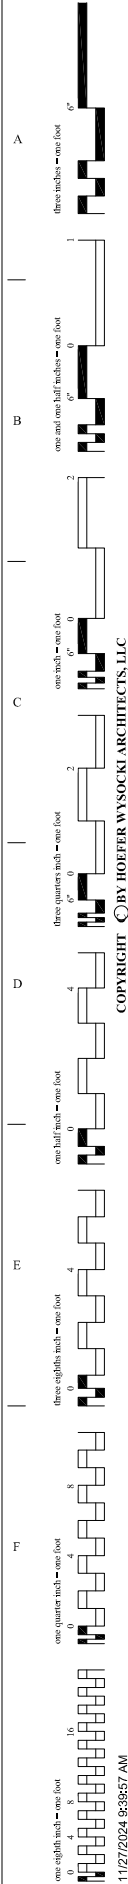


COPYRIGHT © BY HOEFER WYSOCKI ARCHITECTS, LLC

11/27/2024 9:36:57 AM



1 OVERALL NEW B-100 FIRST FLOOR PLAN

NTS

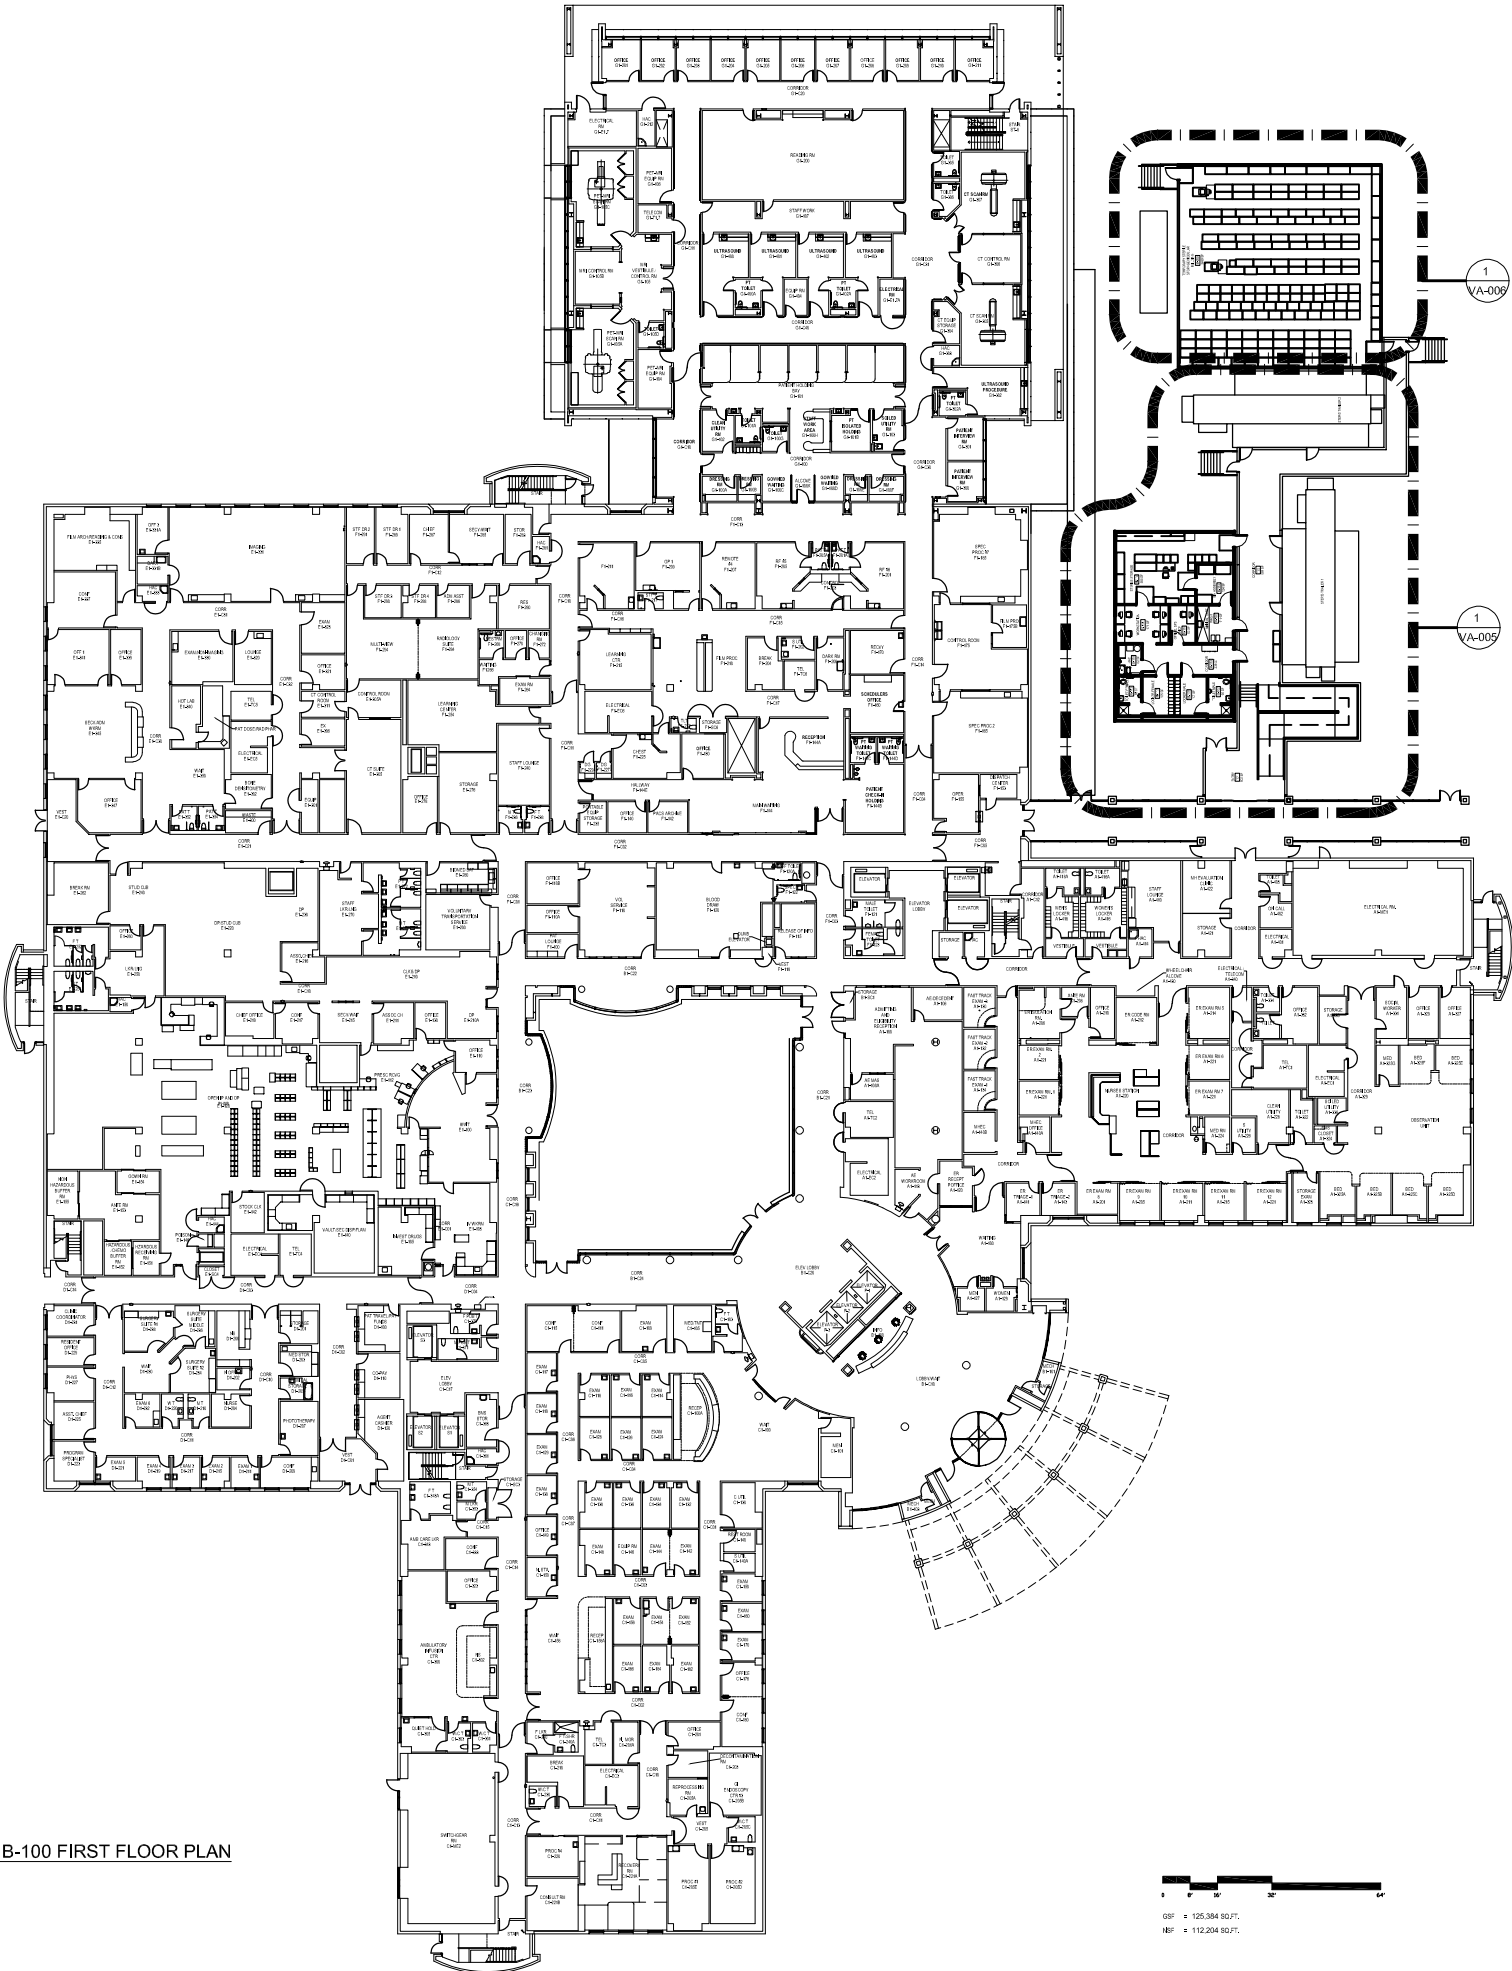

GSF = 125,384 GSF.
NEF = 112,204 GSF.

Office of Facility Planning and Development VA

Project Title
VA Palo Alto - SPS/ SCS Renovation

City of Palo Alto
Santa Clara County, CA
Building Number
100
Project Number:
640-23-108

SHEET NOTES

FF&E PLAN
PHASE I

Revision:	Issue Date
END-USERS SIGN-OFF	05/09/2025
BACKCHECK 1	09/30/2025

Drawing Title:
Overall New B-100 First Floor Plan

Reference To:

Scale:
SEE DWG.
Date:
05/09/25

Drawing Number:
VA-002

Office of
Facility
Planning and
Development

VA

Project Title
VA Palo Alto - SPS/SCS Renovation

City of Palo Alto
Santa Clara County, CA
Building Number
100

Project Number:
640-23-108

SHEET NOTES

FF&E PLAN
PHASE I

Revision	Issue Date
END-USERS SIGN-OFF	05/09/2025
BACKCHECK 1	09/30/2025

Drawing Title:
Enlarged Partial Existing B-100
Basement Floor Plan

Reference To:

Scale:
SEE DWG.
Date:
05/09/25
Drawing Number:
VA-004A

GENERAL NOTES:

- COORDINATE WITH VA PMs FOR EQUIPMENT AND FURNITURE THAT ARE DISCOVERED IN FIELD; YET, THEY ARE NOT ADDRESSED HERE IN THIS DRAWING
- COORDINATE WITH VA PMs IN TAKING CARE OF INSTRUMENTS AND OTHER SMALL ITEMS THAT ARE NOT ADDRESSED HERE IN THIS DRAWING. SMALL ITEMS SUCH AS PORTABLE LIGHTS ON TABLES, OFFICE STATIONERY, COMPUTER, MOUSE, ITEMS ON TABLES, ETC.

SHEET NOTES:

(E) CASEWORK TO BE EXCESS-

- RELOCATE EXISTING STERILIZER CABINET TO SPS MODULAR BUILDING 1 ROOM M-114. SEE SHEET 1/VA-005. MIGHT REQUIRE UN-ANCHORING
- RELOCATE EXISTING DRYING CABINET TO SPS MODULAR BUILDING 1 ROOM M-114. SEE SHEET 1/VA-005. MIGHT REQUIRE UN-ANCHORING
- RELOCATE EXISTING (4) SPS OMNICELLS TO SPS MODULAR BUILDING 1 ROOM M-114. SEE SHEET 1/VA-005
- RELOCATE EXISTING (13) SPS OMNICELLS TO TEMPORARY STERILE STORAGE SPS MODULAR BUILDING 2. SEE SHEET 1/VA-006
- RELOCATE EXISTING (70) SPS STERILE METRO RACKS TO TEMPORARY STERILE STORAGE SPS MODULAR BUILDING 2. SEE SHEET 1/VA-006. THE NUMBERING CORRESPONDS TO THE NEW POSITIONS AT TEMP. MODULAR BUILDING.
- RELOCATE EXISTING (76) SCS RACKS TO STORAGE FB-360, SCS TEMP. STORAGE ROOM GB-103, AND STORAGE ROOM FB-220. SEE SHEET 1/VA-010, 1/VA-008, AND 1/VA-009. THE NUMBERING CORRESPONDS TO THE NEW POSITIONS IN STORAGE RM., IN ROOM FB-360, GB-103, AND IN ROOM FB-220.
- RELOCATE EXISTING (14) SCS CRASH CARTS TO SCS TEMP. STORAGE ROOM GB-101. SEE SHEET 1/VA-008.
- RELOCATE EXISTING (1) SCS UNDERCOUNTER REFRIGERATOR TO SCS TEMP. STORAGE ROOM GB-103. SEE SHEET 1/VA-008.
- RELOCATE EXISTING (1) SCS 3-CELL OMNICELLS TO SCS TEMP. STORAGE ROOM GB-101. SEE SHEET 1/VA-008.
- RELOCATE EXISTING (63) SPS CASE CARTS TO SPS MODULAR BUILDING 1 ROOM M-113 AND TEMPORARY STERILE STORAGE SPS MODULAR BUILDING 2. SEE SHEET 1/VA-005, 1/VA-006.
- NOT USED
- RELOCATE (45) EXISTING SPS WIRE CARTS TO TEMPORARY STERILE STORAGE SPS MODULAR BUILDING 2. SEE SHEET 1/VA-006
- RELOCATE STACKS OF EXISTING SPS RED/BLUE BINS TO SPS MODULAR BUILDING 1 ROOM M-114. SEE SHEET 1/VA-005
- RELOCATE (3) EXISTING SCS METRO CARTS TO STORAGE FB-360. SEE SHEET 1/VA-010
- (E) TRANSFER CARTS TO BE EXCESS-
- (E) (4) COMPACT LOW-TEMP. STERILIZERS TO BE EXCESS- THESE STERILIZERS DO NOT REQUIRE PLUMBING DISCONNECTIONS. THEY MIGHT BE REQUIRED-
- (E) (E) METRO RACKS IN SPS PREP ASSM STER AREA TO BE EXCESS. (E) LABEL PRINTERS AND (E) DOCUMENT SCANNER ON ONE OF THE RACKS TO BE RELOCATED TO TEMP. PREP & PACK TABLES LOCATED IN STERIS TRAILERS. SEE SHEET 2 & 3/VA-007
- (E) (E) INCUBATOR SUPPLIES CABINET TO BE DEMOLISHED. (E) SEAL MACHINE ON THE CABINET TO BE RELOCATED TO TEMP. PREP & PACK TABLES LOCATED IN STERIS TRAILERS. SEE SHEET 2 & 3/VA-007
- (E) (E) (E) CONVEYOR TO BE EXCESS. WORK ON UN-ANCHORING TO BE PERFORMED BY CONSTRUCTION GENERAL CONTRACTOR-
- (E) (E) PREP & PACK TABLES TO BE EXCESS; (E) COMPUTERS AND THEIR ACCESSORIES, (E) HAND-HELD SCANNERS, (E) DOCUMENT SCANNERS, (E) SEAL MACHINES, AND OTHER EQUIPMENT ON (E) PREP & PACK TABLES SHALL BE RELOCATED TO TEMP. PREP & PACK TABLES LOCATED IN STERIS TRAILERS. SEE SHEET 2 & 3/VA-007
- (E) (E) UPPER CABINET TO BE EXCESS-
- (E) (E) WHITE BOARD AND OTHER (E) FURNITURE (DESKS, CHAIRS, CALENDAR BOARDS, A PARTITION, FILE CABINETS, LATERAL FILE CABINETS, PEDESTALS, TACK BOARDS, WHITE BOARDS, BOOKCASES, GLASS CASES, CLOCKS, ETC.) TO BE UN-INSTALLED IF NECESSARY & RELINQUISHED TO VAPA FURNITURE CONTRACTOR
- (E) (E) (E) MED. TEMP. STERILIZERS TO BE EXCESS. WORK ON UN-ANCHORING AND DISCONNECTIONS TO BE PERFORMED BY CONSTRUCTION GENERAL CONTRACTOR-
- (E) (E) SEAL MACHINE(S) TO BE RELOCATED TO TEMP. PREP & PACK TABLES LOCATED IN TEMP. STERIS TRAILERS. SEE SHEET 2 & 3/VA-007
- (E) (E) (E) (1) COMPUTER WORKSTATION TO BE RELINQUISHED TO VAPA O&T
- (E) (E) (E) SANITARY EQUIPMENT (E) TRASHES, (E) SHARP CONTAINERS, ETC.) TO BE RELINQUISHED TO VAPA EMS
- (E) (E) MISC. IT EQUIPMENT TO BE RELINQUISHED TO VAPA O&T
- (E) (E) MISC. IT EQUIPMENT TO BE RELOCATED TO TEMP. PREP & PACK TABLES LOCATED IN STERIS TRAILERS. SEE SHEET 2 & 3/VA-007
- (E) (E) SCS SUPPLIES WILL BE TAKEN CARE OF BY SCS END USERS
- (E) (E) MISC. EQUIPMENT TO BE EXCESS-
- (E) (E) HUDDLE BOARD TO BE RELOCATED TO SPS MODULAR BUILDING 1 CORRIDOR M-119. SEE SHEET 1/VA-005. REQUIRES UN-ANCHORING
- (E) (E) (E) (2) CENSITRAC COMPUTER WORKSTATIONS AND THEIR ACCESSORIES TO BE RELOCATED TO TEMPORARY STERILE STORAGE SPS MODULAR BUILDING 2. SEE SHEET 1/VA-006
- (N) CENSITRAC WILL BE INSTALLED AT MODULAR #2



1 ENLARGED PARTIAL EXISTING B-100 BASEMENT FLOOR PLAN IN SPS/SCS SUITE
1/4" = 1'-0"

Office of
Facility
Planning and
Development
VA

Project Title
VA Palo Alto - SPS/ SCS Renovation

City of Palo Alto
Santa Clara County, CA

Building Number
100

Project Number:
640-23-108

SHEET NOTES

FF&E PLAN
PHASE I

Revision	Issue Date
END-USERS SIGN-OFF	05/09/2025
BACKCHECK 1	09/30/2025

Enlarged Partial Existing B-100
Basement Room SPS Offices &
Lounge, Decont., and SPS/ SCS
Locker Rooms Floor Plans


Scale:
SEE DWG.
Date:
05/09/25
Drawing Number:
VA-004B

GENERAL NOTES:


- COORDINATE WITH VA PMs FOR EQUIPMENT AND FURNITURE THAT ARE DISCOVERED IN FIELD; YET, THEY ARE NOT ADDRESSED HERE IN THIS DRAWING
- COORDINATE WITH VA PMs IN TAKING CARE OF INSTRUMENTS AND OTHER SMALL ITEMS THAT ARE NOT ADDRESSED HERE IN THIS DRAWING. SMALL ITEMS SUCH AS PORTABLE LIGHTS ON TABLES, OFFICE STATIONERY, COMPUTER, MOUSE, ITEMS ON TABLES, ETC.

SHEET NOTES:


- ALL EXISTING FURNITURE (DESKS, CHAIRS, CALENDAR BOARDS, A PARTITION, FILE CABINETS, LATERAL FILE CABINETS, PEDESTALS, TACK BOARDS, WHITE BOARDS, BOOKCASES, GLASS CASES, CLOCKS, ETC.) TO BE UNINSTALLED IF NECESSARY & RELINQUISHED TO VAPA FURNITURE CONTRACTOR
- MISC. EQUIPMENT TO BE EXCESS
- EXISTING (2) SPS METRO RACKS TO BE USED FOR PPE TO BE RELOCATED TO NEW CORRIDOR 102; SEE SHEET 1/VA-005
- EXISTING (2) SANITARY EQUIPMENT ((E) TRASHES, (E) SHARP CONTAINERS, ETC.) TO BE RELINQUISHED TO VAPA EMS
- MISC. IT EQUIPMENT TO BE RELINQUISHED TO VAPA O&T
- (E) (4) COMPUTERS AND THEIR ACCESSORIES ARE TO BE RELOCATED TO TEMPORARY STERILE STORAGE SPS MODULAR BUILDING 1 ROOM M-115. SEE SHEET 1/VA-005
- EXISTING VERTICAL BARS TO SUPPORT EXISTING WORKSTATION IN ROOM EB-370 TO BE DEMOLISHED
- NOT USED
- RELOCATE EXISTING (1) SPS OMNICELLS TO TEMPORARY STERILE STORAGE SPS MODULAR BUILDING 1 ROOM M-114; SEE SHEET 1/VA-005
- RELOCATE EXISTING (1) ETCHING MACHINE WITH ITS (2) COMPUTERS MOUNTED ON WALL, AND THEIR ACCESSORIES, AND THEIR MONITOR ARMS, AND EVERYTHING IN THIS ROOM (EXCEPT AIR TANK, TRASH CANS, CARTS, CASE CART, AND EYE WASH STN) TO STORAGE EB-250. SEE SHEET 1/VA-007. THIS EQUIPMENT REQUIRES DISASSEMBLING AND ASSEMBLING AFTER THE MOVE TO THE NEW SPACE, UN-ANCHORING, AND PLUMBING DISCONNECTION
- EXISTING FLASH LIGHT(S) TO BE EXCESS. REQUIRES UN-ANCHORING
- (1) (E) CHECK IN WORKSTATION TO BE RELOCATED TO TEMPORARY STERILE STORAGE SPS MODULAR BUILDING 1 ROOM M-114. SEE SHEET 1/VA-005 - ONLY THE COMPUTER, KEYBOARD, MOUSE, SCALE, AND THE LABEL PRINTER, FOR THE (E) S.S. DRAWER AND PLASTIC DRAWER CABINET AND COMPUTER MONITOR ARM. RELINQUISH THEM TO VAPA FURNITURE CONTRACTOR. THIS WORK REQUIRES UN-ANCHORING
- EXISTING MIRRORS TO BE EXCESS. THIS WORK REQUIRES UN-ANCHORING
- EXISTING LOCKER BENCHES AND LOCKERS TO BE DEMOLISHED
- EXISTING ARTWORK(S) TO BE RELINQUISHED TO VAPA FURNITURE CONTRACTOR. THIS WORK REQUIRES UN-ANCHORING
- EXISTING (3) WASHERS AND (1) CART WASHER MACHINES TO BE EXCESS. DISCONNECTIONS AND UN-ANCHORING WILL BE PERFORMED BY CONSTRUCTION GENERAL CONTRACTOR
- EXISTING TRANSFER CARTS AND OTHER SPS METRO RACKS TO BE EXCESS
- EXISTING (1) CONVEYOR TO BE EXCESS. WORK ON UN-ANCHORING TO BE PERFORMED BY CONSTRUCTION GENERAL CONTRACTOR
- EXISTING (2) REPROCESSING SINKS AND (3) ULTRASONIC CLEANERS TO BE EXCESS. WORK ON UN-ANCHORING & DISCONNECTIONS TO BE PERFORMED BY CONSTRUCTION GENERAL CONTRACTOR
- EXISTING (2) STAINLESS STEEL BIG TABLES TO BE RELINQUISHED TO VAPA FURNITURE CONTRACTOR
- (1) EXISTING WALL MOUNTED COMPUTER AND ITS ACCESSORIES, EXCEPT ITS MONITOR ARM, TO BE RELOCATED TO O.R. STERIS TRAILER. SEE SHEET 2/VA-007. RELINQUISH EXISTING COMPUTER MONITOR ARM TO VAPA FURNITURE CONTRACTOR. THIS WORK REQUIRES UN-ANCHORING STERIS TRAILER COW
- (1) EXISTING WALL MOUNTED COMPUTER AND ITS ACCESSORIES TO BE RELOCATED TO O.R. STERIS TRAILER. SEE SHEET 2/VA-007. THIS WORK REQUIRES UN-ANCHORING STERIS TRAILER WALL MOUNTED
- EXISTING (2) DENTAL LUBRICATIONS AND THEIR ACCESSORIES, AND ITS TANK PUMP TO BE RELOCATED TO EYE/ DENTAL STERIS TRAILER. SEE SHEET 3/VA-007. THIS ONE NEEDS A DISCONNECTION AND UN-ANCHORING WORK
- EXISTING PPE CABINETS TO BE RELINQUISHED TO VAPA FURNITURE CONTRACTOR.
- EXISTING PPE RACK TO BE EXCESS
- NOT USED
- EXISTING COAT HOOKS TO BE EXCESS
- (E) (1) COMPUTER AND ITS ACCESSORIES IS TO BE RELOCATED TO TEMPORARY STERILE STORAGE SPS MODULAR BUILDING 1 ROOM M-115. SEE SHEET 1/VA-005
- (E) KEY LOCK CABINET TO BE RELOCATED TO TEMPORARY STERILE STORAGE SPS MODULAR BUILDING 1 ROOM M-115. SEE SHEET 1/VA-005. THIS REQUIRES UN-ANCHORING
- (1) EXISTING WALL MOUNTED COMPUTER AND ITS ACCESSORIES TO BE RELOCATED TO EYE/ DENTAL STERIS TRAILER. SEE SHEET 3/VA-007. THIS WORK REQUIRES UN-ANCHORING STERIS TRAILER WALL MOUNTED
- (E) (2) CIDEXs ON CARTS TO BE RELOCATED TO BOTH TEMP. STERIS TRAILERS. SEE SHEET 2 & 3/VA-007. RELOCATE THE CIDEXs AND THEIR COMPONENTS TO THE NEW CARTS
- (E) SPS SUPPLIES WILL BE TAKEN CARE OF BY SPS END USERS
- (E) CASEWORK AND UPPER CABINET IN EXISTING LOUNGE EB-358 TO BE DEMOLISHED
- (1) EXISTING WALL MOUNTED COMPUTER AND ITS ACCESSORIES, EXCEPT ITS MONITOR ARM, TO BE RELOCATED TO EYE/ DENTAL STERIS TRAILER. SEE SHEET 3/VA-007. RELINQUISH EXISTING COMPUTER MONITOR ARM TO VAPA FURNITURE CONT. THIS WORK REQUIRES UN-ANCHORING STERIS TRAILER COW

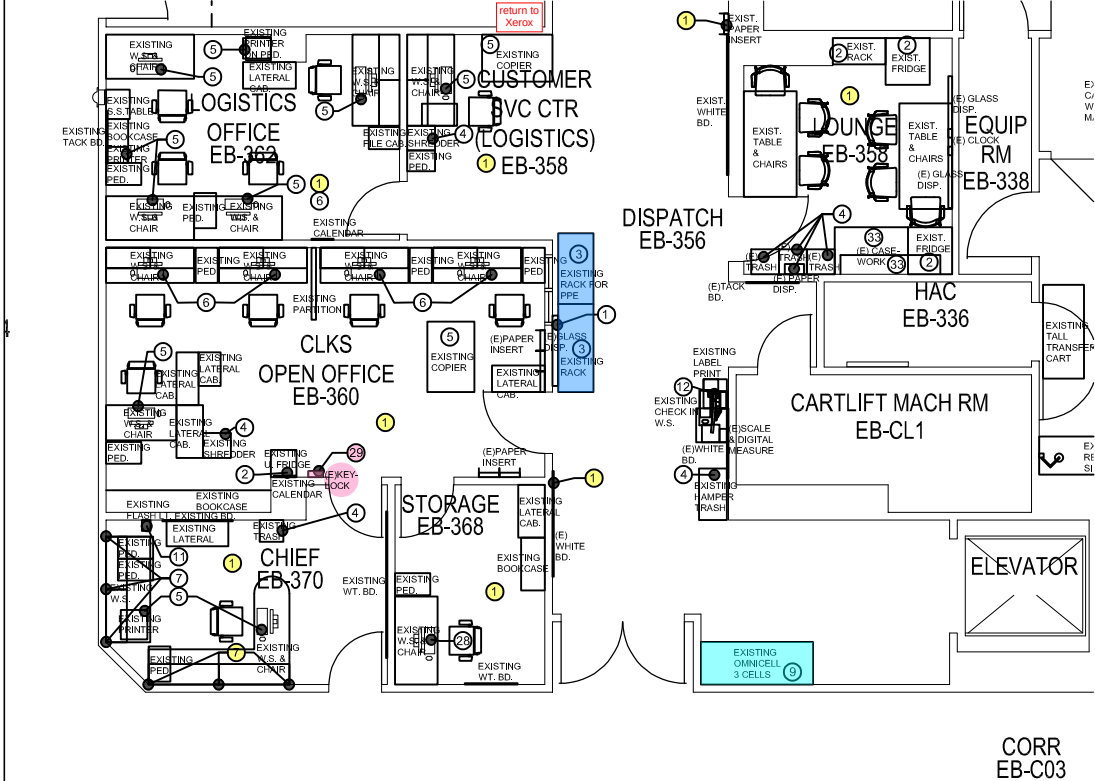


1 ENLARGED PARTIAL EXISTING B-100 BASEMENT IN SPS/ SCS OFFICES FLOOR PLAN

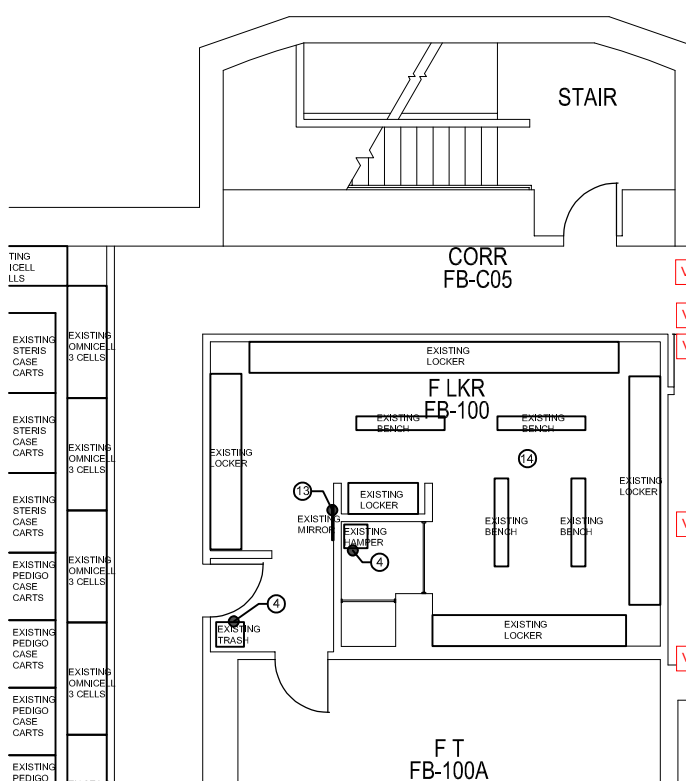

2 ENLARGED PARTIAL EXISTING B-100 BASEMENT IN SPS/ SCS FEMALE LOCKER FLOOR PLAN

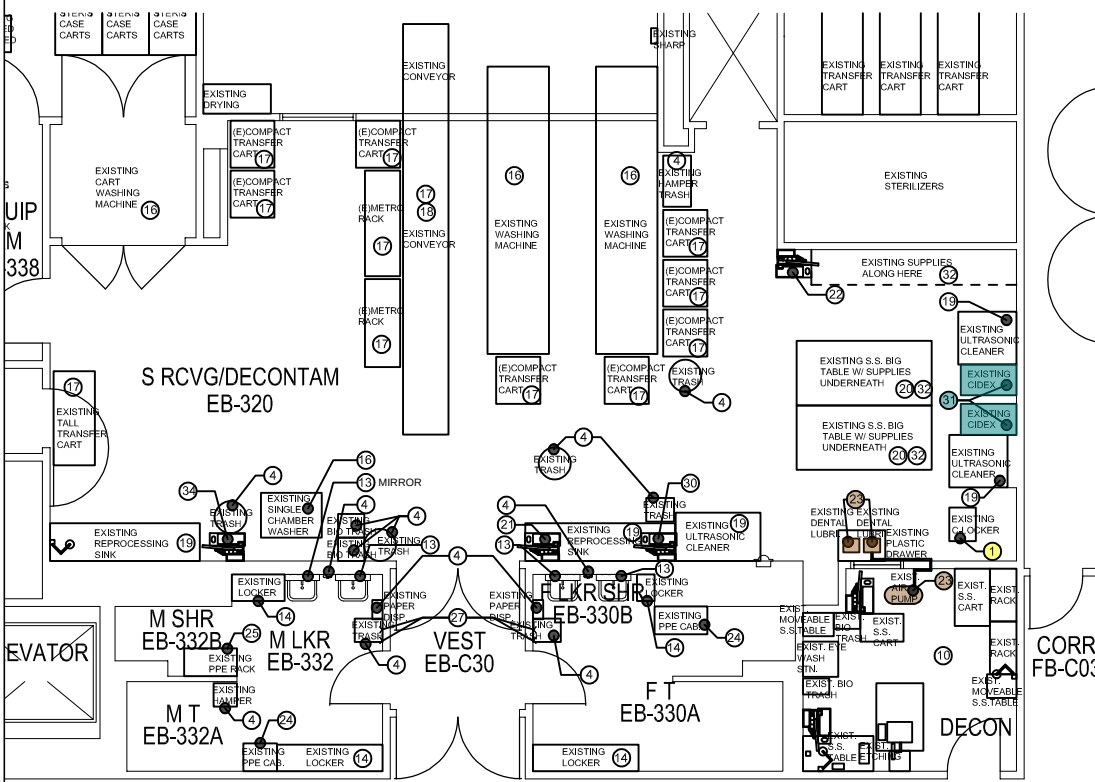

3 ENLARGED PARTIAL EXISTING B-100 BASEMENT IN SPS DECONT. AREA FLOOR PLAN

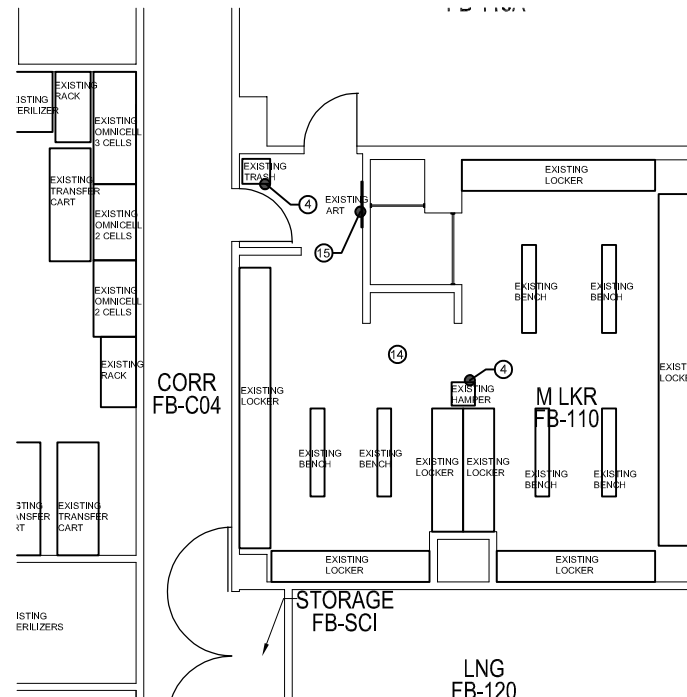

4 ENLARGED PARTIAL EXISTING B-100 BASEMENT IN SPS/ SCS M LOCKER FLOOR PLAN

Office of
Facility
Planning and
Development
VA

Project Title
VA Palo Alto - SPS/ SCS Renovation

City of Palo Alto
Santa Clara County, CA
Building Number
100
Project Number:
640-23-108


SHEET NOTES

FF&E PLAN
PHASE I

Revision:	Issue Date
END-USERS SIGN-OFF	05/09/2025
BACKCHECK 1	09/30/2025

Drawing Title:
Enlarged Partial Existing B-100
Basement Room FB-360 and
FB-220

Scale: SEE DWG.	Drawing Number: VA-004C
Date: 05/09/25	

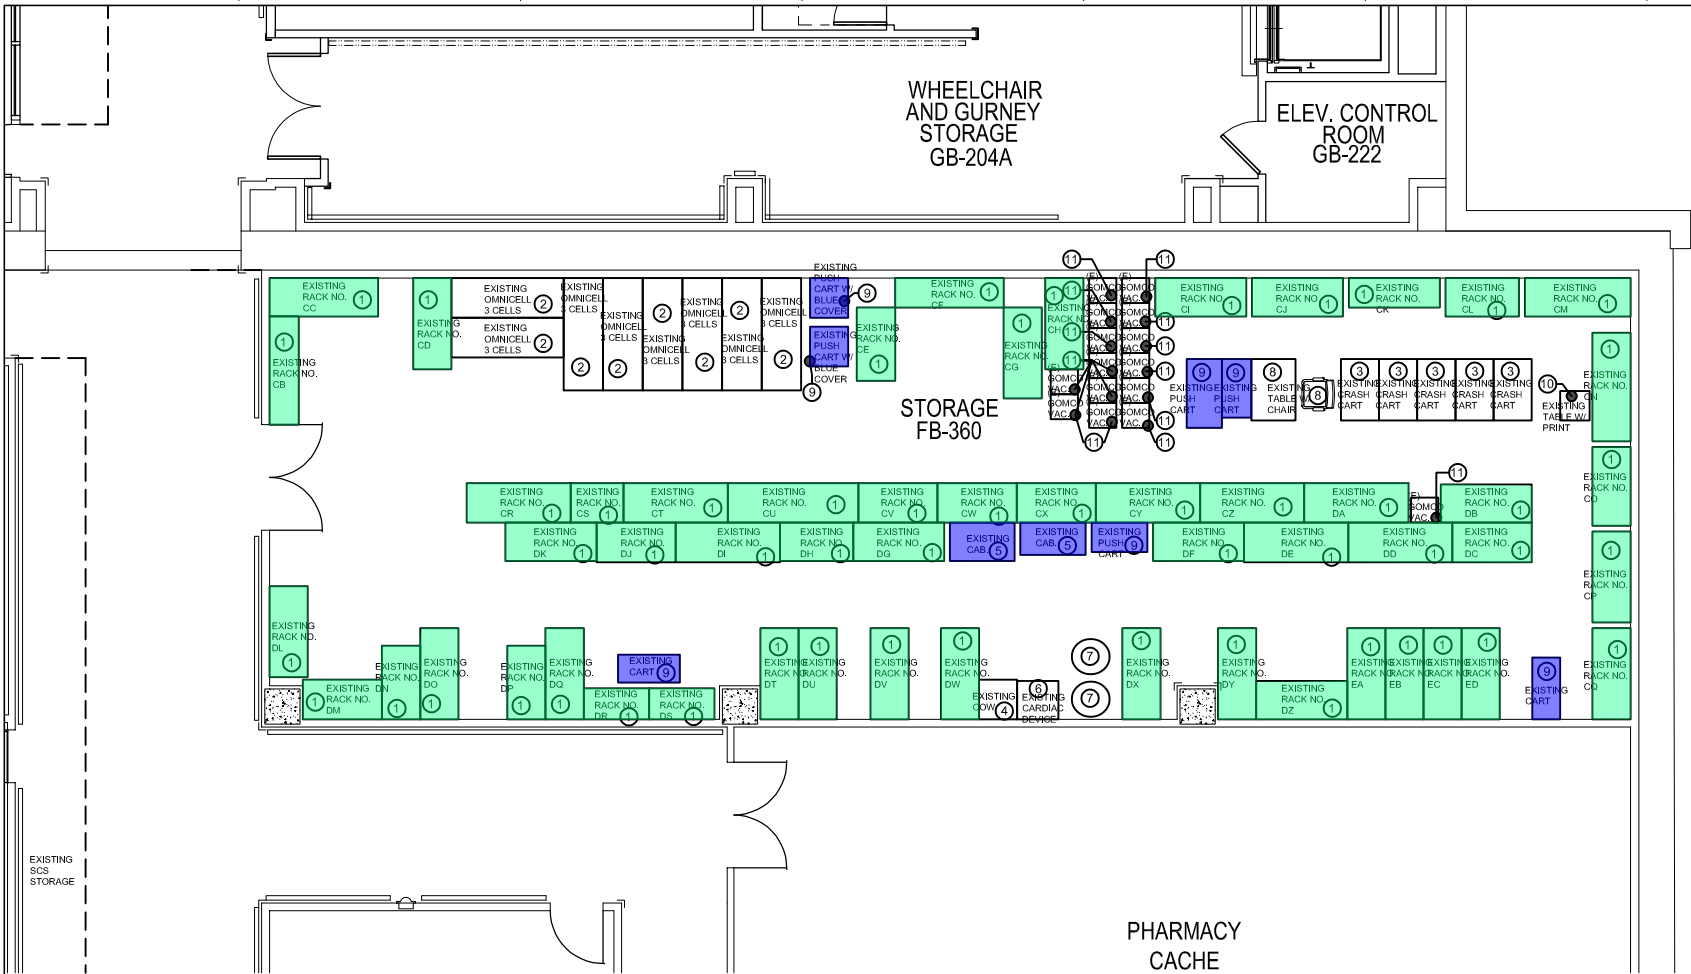

1 ENLARGED PARTIAL EXISTING B-100 BASEMENT ROOM FB-360 FLOOR PLAN
1/8" = 1'-0"

GENERAL NOTES:

- COORDINATE WITH VA PMs FOR EQUIPMENT AND FURNITURE THAT ARE DISCOVERED IN FIELD; YET, THEY ARE NOT ADDRESSED HERE IN THIS DRAWING
- COORDINATE WITH VA PMs IN TAKING CARE OF INSTRUMENTS AND OTHER SMALL ITEMS THAT ARE NOT ADDRESSED HERE IN THIS DRAWING. SMALL ITEMS SUCH AS PORTABLE LIGHTS ON TABLES, OFFICE STATIONERY, COMPUTER, MOUSE, ITEMS ON TABLES, ETC.

SHEET NOTES:

- RELOCATE (56) EXISTING SCS RACKS TO SCS TEMP. TRAILER. SEE SHEET 2VA-006. THE NUMBERING CORRESPONDS TO THE NEW POSITIONS IN TEMP. TRAILER
- EXISTING (8) OMNICELL CABINETS TO REMAIN
- EXISTING (5) CRASH CARTS TO REMAIN
- EXISTING (1) COMPUTER ON WHEEL TO REMAIN
- EXISTING (2) TALL CABINETS TO BE RELOCATED TO SCS TEMP. TRAILER. SEE SHEET 2VA-006

- VA 6 EXISTING (1) CARDIAC DEVICE TO BE REMOVED PER SCS END USERS
- VA 7 EXISTING (2) MISC. EQUIPMENT TO BE REMOVED PER SCS END USERS

- VA 8 EXISTING (1) CHAIR AND (1) DESK TO BE REMOVED PER SCS END USERS

- 9 RELOCATE EXISTING SCS CARTS TO SCS TEMP. TRAILER. SEE SHEET 2VA-006.

- VA 10 EXISTING (1) PRINTER DESK AND (1) PRINTER TO BE REMOVED PER SCS END USERS

- VA 11 EXISTING VACUUM EQUIPMENT TO BE REMOVED PER SCS END USERS


- VA 12 EXISTING SCS PALLETS TO BE REMOVED PER SCS END USERS

- 13 EXISTING METAL SHELVING TO REMAIN

- 14 EXISTING SCS RACKS TO REMAIN

- 15 EXISTING SCS CABINETS TO REMAIN

- 16 EXISTING CART TO REMAIN

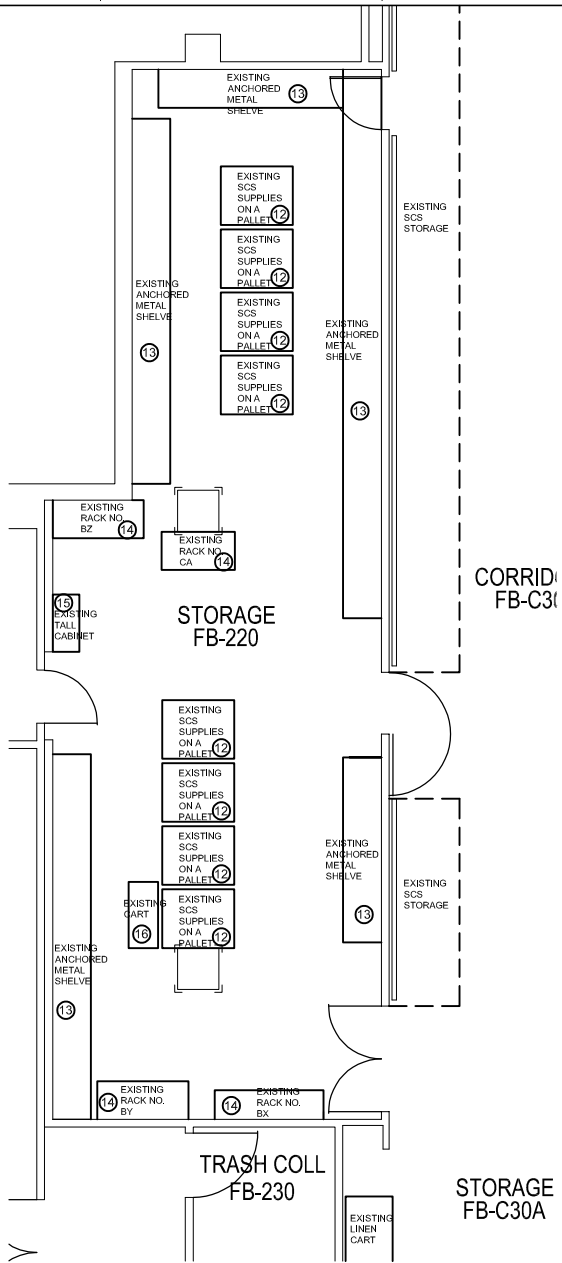

2 ENLARGED PARTIAL EXISTING B-100 BASEMENT ROOM FB-220 FLOOR PLAN
1/8" = 1'-0"

- LEGEND:**
- A1030** INDICATE NEW EQUIPMENT AND FURNITURE. REFER TO EQUIPMENT AND FURNITURE SCHEDULE ON 1/VA-011
- NEW PROPOSED LOCATIONS OF ADDITIONAL POWER AND DATA**
- NEW PROPOSED LOCATIONS OF ADDITIONAL EMERGENCY POWER**

SHEET NOTES:


- 1 (2) EXISTING SPS 2-CELLS OMNICELLS THAT ARE RELOCATED FROM EXISTING PREP ASSM STER ROOM EB-312. SEE 1/VA-011 FOR ADDITIONAL INFO
- 2 (2) EXISTING SPS 3-CELLS OMNICELLS THAT ARE RELOCATED FROM EXISTING PREP ASSM STER ROOM EB-312. SEE 1/VA-011 FOR ADDITIONAL INFO
- 3 EXISTING LOWER AND UPPER CABINET THAT IS RELOCATED FROM EXISTING PREP ASSM STER ROOM EB-312. SEE 1/VA-011 FOR ADDITIONAL INFO
- 4 EXISTING STETHOSCOPE CABINET THAT IS RELOCATED FROM EXISTING PREP ASSM STER ROOM EB-312. SEE 1/VA-011 FOR ADDITIONAL INFO
- 5 EXISTING DRYING CABINET THAT IS RELOCATED FROM EXISTING PREP ASSM STER ROOM EB-312. SEE 1/VA-011 FOR ADDITIONAL INFO

SHEET NOTES (CONTINUED):

- 6 EXISTING (3) SPS CASE CARTS RELOCATED FROM EXISTING CART WASH AREA EB-340A, EQ TEST EB-340, STER/NOH STER STOR EB-300, AND CORRIDOR EB-C40. SEE 1/VA-011 FOR ADDITIONAL INFO
- 7 EXISTING STACKS OF SPS RED/ BLUE BINS RELOCATED FROM EXISTING CART WASH AREA EB-340A, EQ TEST EB-340. SEE 1/VA-011 FOR ADDITIONAL INFO
- 8 (1) EXISTING SPS 3-CELLS OMNICELL THAT IS RELOCATED FROM EXISTING DISPATCH ROOM EB-356B. SEE 1/VA-011 FOR ADDITIONAL INFO
- 9 (1) (E) CHECK-IN LABEL PRINTER, COMPUTER, KEYBOARD, MOUSE, SCALE, AND ITS DIGITAL MEASURE MOVED FROM (E) DISPATCH EB-356. SEE 1/VA-011 FOR ADDITIONAL INFO
- 10 (E) UPPER CABINET MOVED FROM (E) PREP ASSM STER ROOM. SEE 1/VA-011 FOR ADDITIONAL INFO
- 11 (E) (1) KEYLOCK CABINET MOVED FROM (E) CLKS OPEN OFFICE EB-360. INSTALLATION REQUIRES ANCHORS TO WALL. MT. HT.: 48" A.F.F. TO TOP OF THE CABINET. SEE 1/VA-011 FOR ADDITIONAL INFO
- 12 (E) (2) HIGH PRESSURE STEAMERS SUPPLIED BY THE END-USERS. SEE 1/VA-011 FOR ADDITIONAL INFO

SHEET NOTES (CONTINUED):

- 13 (4) (E) COMPUTERS AND THEIR ACCESSORIES MOVED FROM (E) CLKS OPEN OFFICE EB-360. SEE 1/VA-011 FOR ADDITIONAL INFO
- 14 (E) COMPUTER AND ITS ACCESSORIES MOVED FROM (E) STORAGE EB-368 ROOM. SEE 1/VA-011 FOR ADDITIONAL INFO
- 15 EXISTING (2) SPS METRO RACKS TO BE USED FOR PPE, MOVED FROM (E) DISPATCH EB-356
- 16 EXISTING (1) SPS HUDDLE BOARD MOVED FROM EXISTING DISPATCH EB-356 AREA. SEE 1/VA-011 FOR ADDITIONAL INFO
- 17 EXISTING (1) ERGONOMIC CHECK-IN TABLE WILL BE RELOCATED TO HERE. TABLE WILL BE PROVIDED BY THE END-USERS. SEE 1/VA-011 FOR ADDITIONAL INFO

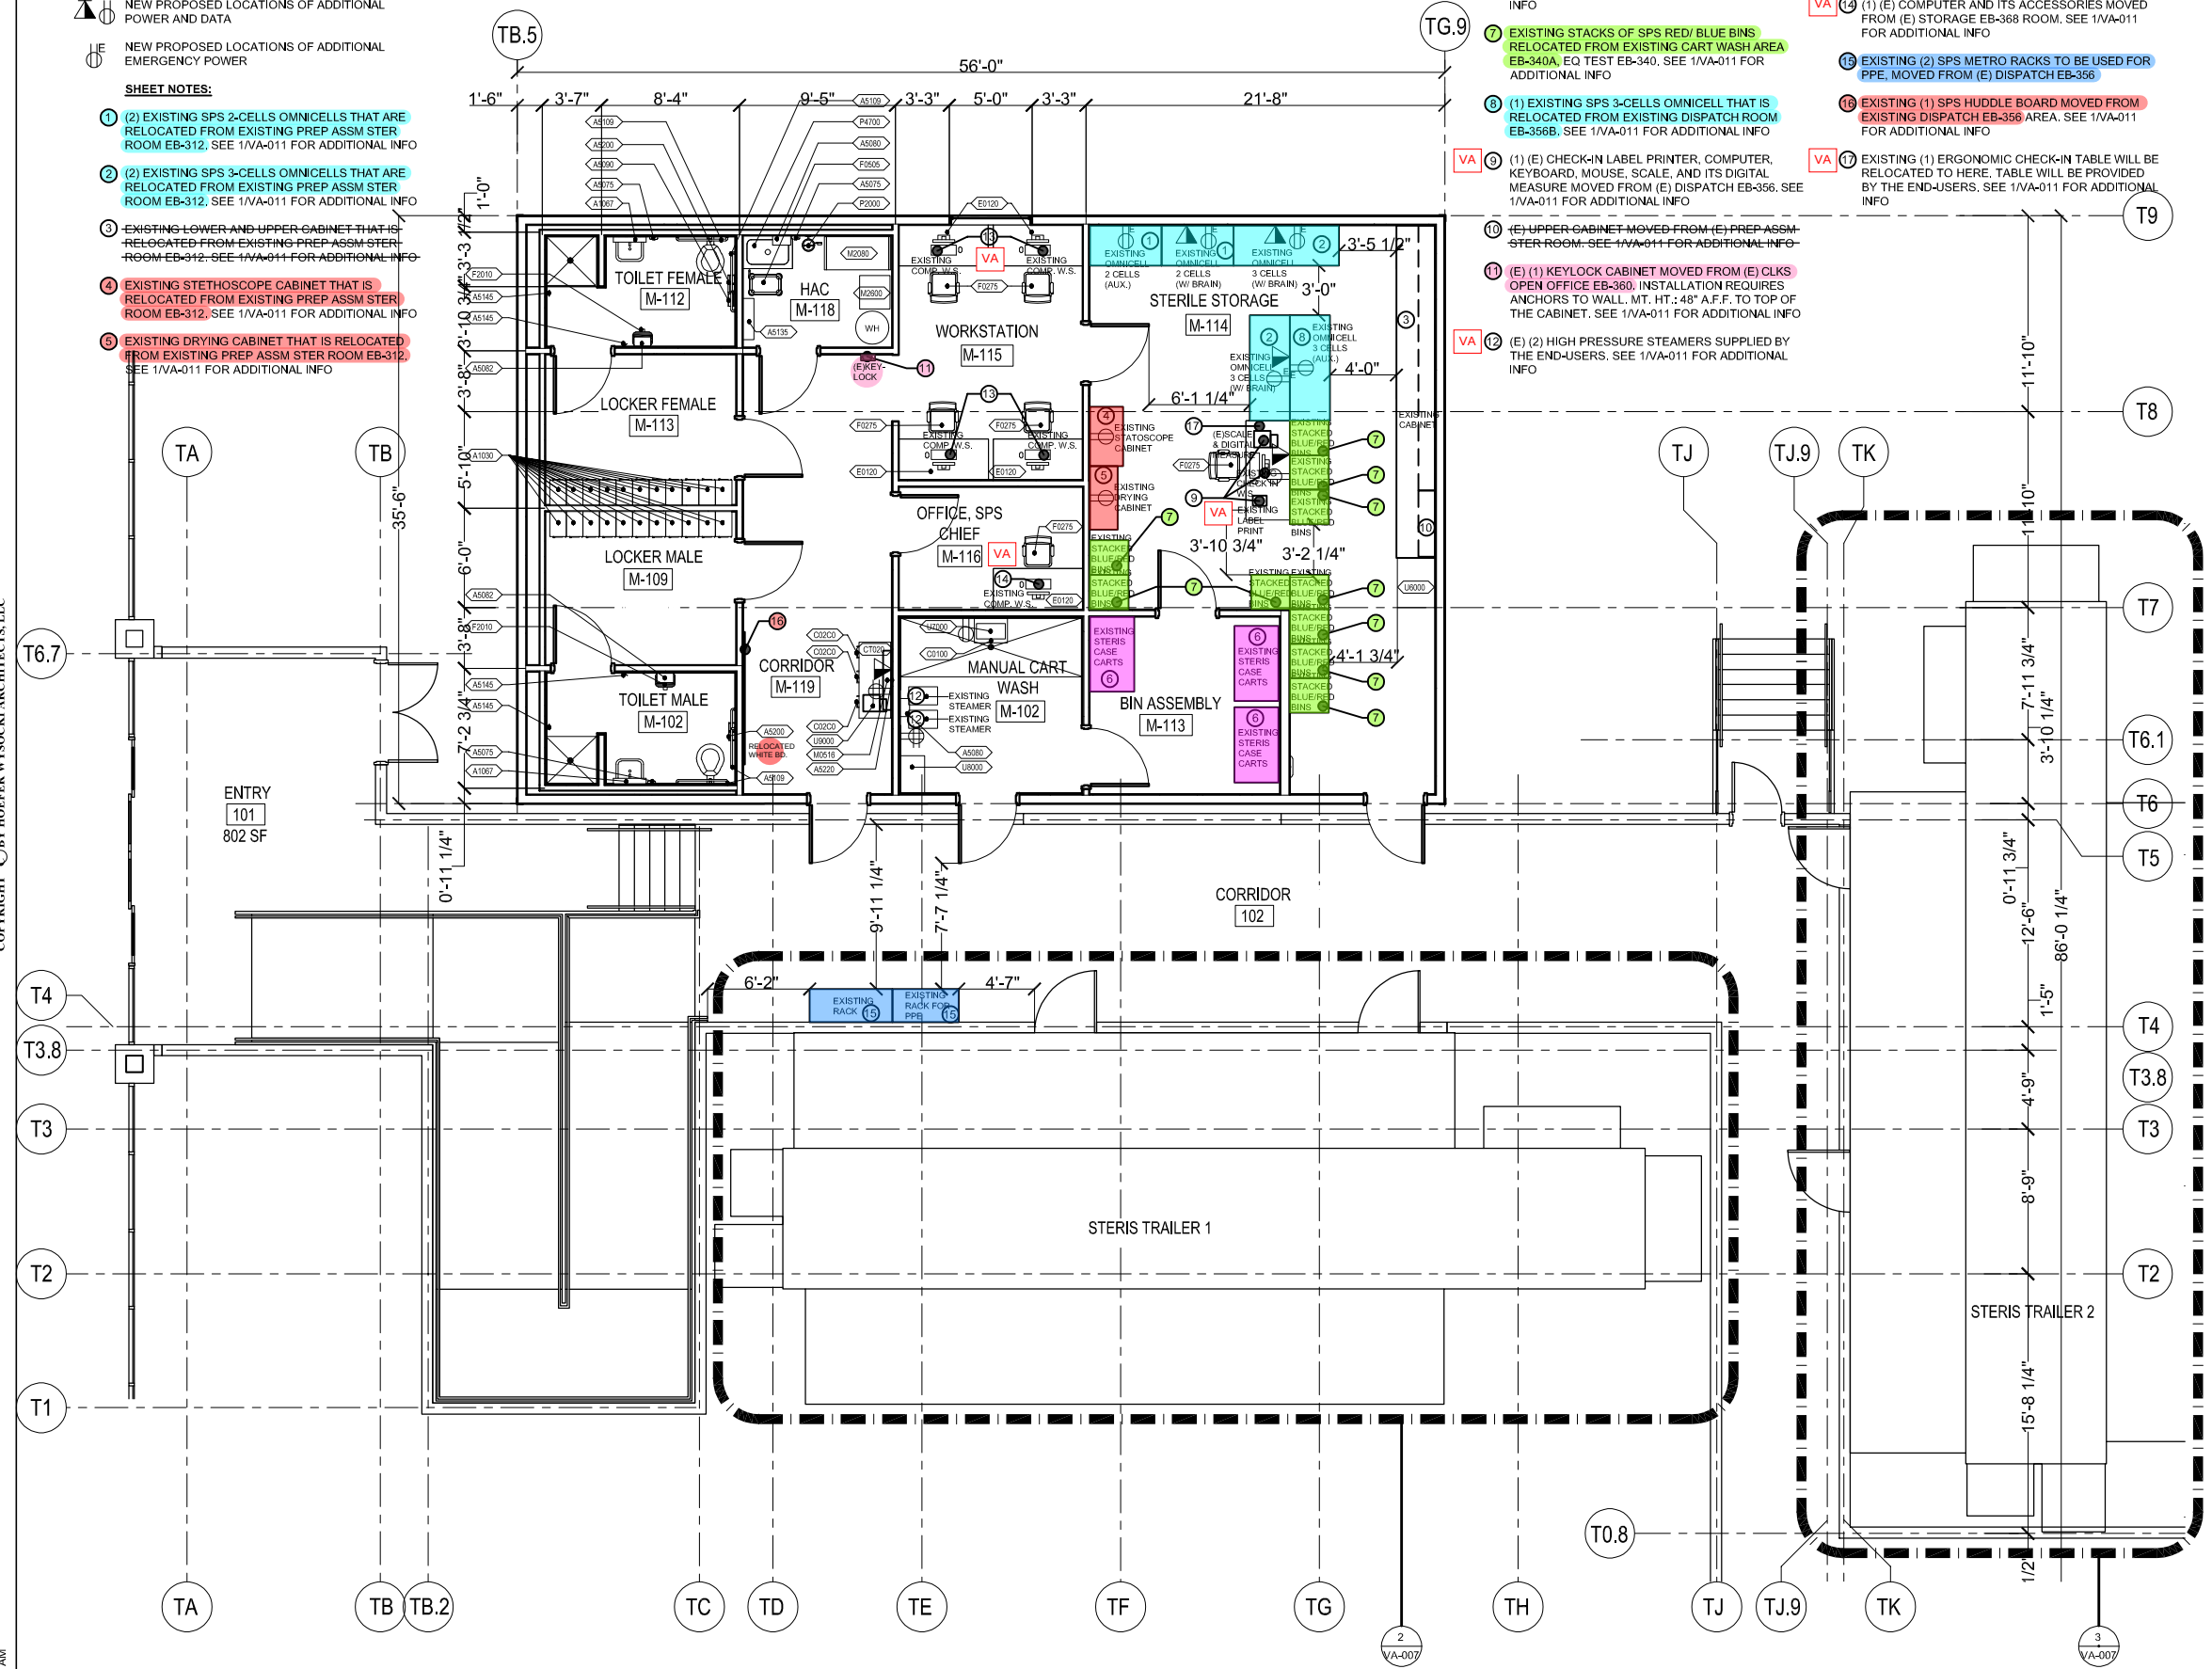

1 NEW SPS TEMP. MODULAR BUILDING 1 FLOOR PLAN

Office of Facility Planning and Development

VA

Project Title
VA Palo Alto - SPS/ SCS Renovation

City of Palo Alto
Santa Clara County, CA
Building Number
100
Project Number:
640-23-108

SHEET NOTES

FF&E PLAN
PHASE I

Revision:	Issue Date
END-USERS SIGN-OFF	05/09/2025
BACKCHECK 1	09/30/2025

Drawing Title:
New SPS Temp. Modular Building 1 Floor Plan

Reference To:	
Scale: SEE DWG.	Drawing Number: VA-005
Date: 05/09/25	

FF&E PLAN
PHASE I

Scale: SEE DWG.	Drawing Number: VA-006
Date: 05/09/25	



COPYRIGHT © BY HOEFER WYSOCKI ARCHITECTS, LLC

11/27/2024 9:39:57 AM




City of Palo Alto
Santa Clara County, CA
Building Number
100
Project Number:
640-23-108

FF&E PLAN
PHASE I[illegible]

Drawing Title:
New SPS Temporary Swing Space
at FB-250 Room & STERIS Trailers
Floor Plans

Reference 10

Scale: SEE DWG.	Drawing Number: VA-007
Date: 05/09/25	

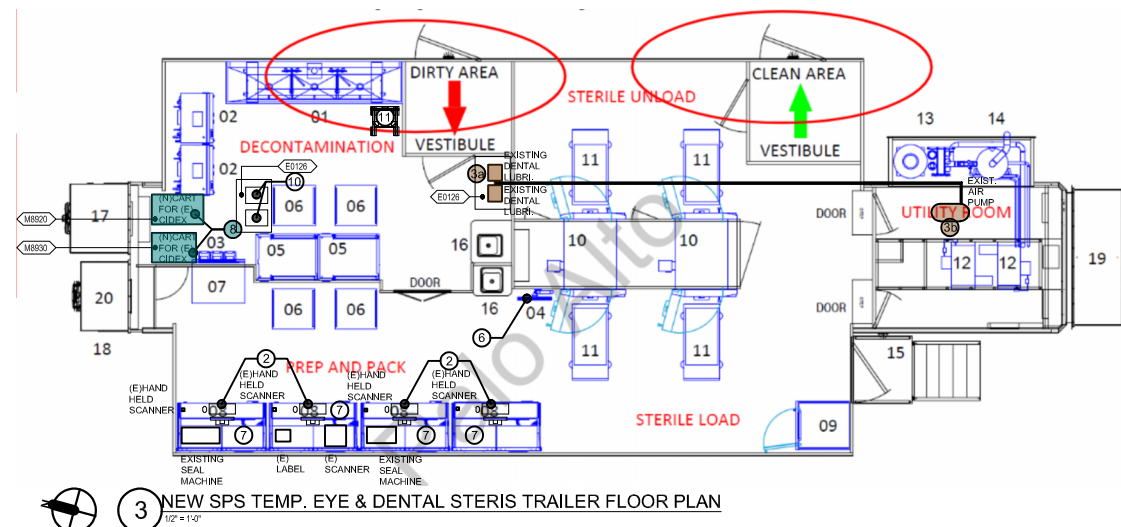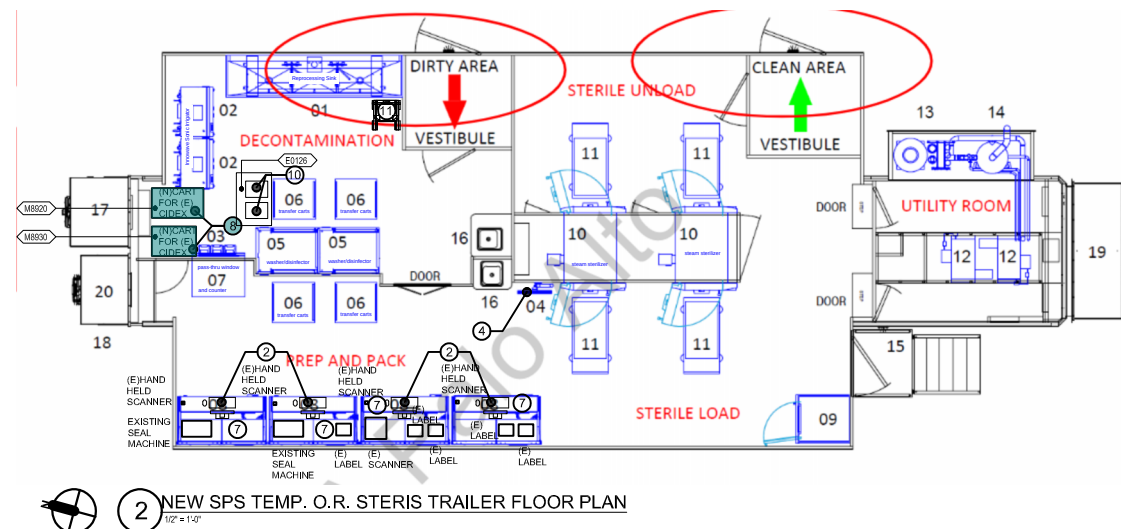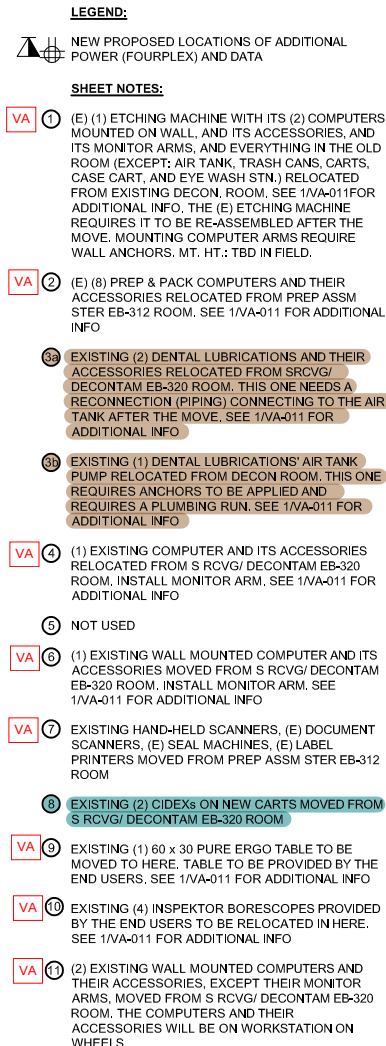



11/27/2024 9:39:57 AM


1

1 NEW SCS TEMP. SWING SPACE AT GB-101 & 103 ROOMS FLOOR PLAN

$$1/2'' = 1'-0''$$
$$1/2'' = 1'-0''$$

4 EXISTING (14) CRASH CARTS RELOCATED FROM EXISTING SCS DECON ROOM. SEE 1/A-011 FOR ADDITIONAL INFO

VA-008

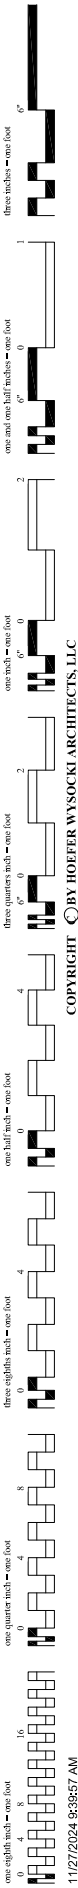

COPYRIGHT © BY HOEFER WYSOCKI ARCHITECTS, LLC

11/27/2024 9:36:57 AM



1 NEW/ EXISTING SCS SPACE IN ROOM FB-220 FLOOR PLAN
3/8" = 1'-0"

VA FORM 08-6231



- SHEET NOTES:**
- 1 EXISTING (1) SCS RACKS RELOCATED FROM EXISTING EQUIP ROOM FB-300B. SEE 1/VA-011 FOR ADDITIONAL INFO

Office of Facility Planning and Development

VA

Project Title
VA Palo Alto - SPS/ SCS Renovation

City of Palo Alto
Santa Clara County, CA

Building Number
100

Project Number:
640-23-108

SHEET NOTES

FF&E PLAN
PHASE I

Revision:	Issue Date
END-USERS SIGN-OFF	05/09/2025
BACKCHECK 1	09/30/2025

Drawing Title:
New/ Existing SCS Space in Room FB-220 Floor Plan

Scale: SEE DWG.	Drawing Number: VA-009
Date: 05/09/25	



Office of
Facility
Planning and
Development
VA

Project Title

VA Palo Alto - SPS/ SCS Renovation

City of Palo Alto
Santa Clara County, CA
Building Number
100
Project Number:
640-23-108

SHEET NOTES

FF&E PLAN
PHASE I

Revision:	Issue Date
END-USERS SIGN-OFF	05/09/2025
BACKCHECK 1	09/30/2025

Drawing Title:

SCS New/ Existing FB-360 Room
Floor Plan

Reference To:

Scale: SEE DWG.	Drawing Number: VA-010
Date: 05/09/25	

EQUIPMENT AND FURNITURE SCHEDULE											
MARK	TYPE	ACQ	QTY	FURN/ EQUIP.	Utilities			BACKING	STATUS (EXIST/ NEW)	REMARKS	
					Plumbing	Electrical	Misc Gas				
A1030	LOCKER, 2 PERSON, OVERSUNDER	C.C.	22	FURN.	-	-	-	YES	NEW	PROVIDE BACKING	
A1067	MIRROR, FLOAT GLASS, W/STAINLESS STEEL FRAME, ADA ACCESSIBLE, 18"x36"	C.C.	2	EQUIP.	-	-	-	YES	NEW	PROVIDE BACKING IF FASTENERS IN BETWEEN STUDS	
A5075	DISPENSER, SOAP, DISPOSABLE	V.V.	3	EQUIP.	-	-	-	-	NO	NEW	
A5080	DISPENSER, PAPER TOWEL, SS, SURFACE MOUNTED	C.C.	2	EQUIP.	-	-	-	-	NO	NEW	
A5082	DISPENSER, PAPER TOWEL, SENSOR, HANDS FREE	C.C.	2	EQUIP.	-	-	-	-	NO	NEW	
A5090	DISPOSAL, SANITARY NAPKIN, STAINLESS STEEL, SURFACE MOUNTED	C.C.	1	EQUIP.	-	-	-	-	NO	NEW	
A5109	GRAB BAR, 1 1/4" DIA., SS, 2 WALL, W/C ACCESSIBLE	C.C.	4	EQUIP.	-	-	-	YES	NEW	PROVIDE BACKING	
A5135	SHELF, UTILITY W/ MOP/ BROOM HOLDERS, SS, SURF MNTD	C.C.	1	EQUIP.	-	-	-	YES	NEW	PROVIDE BACKING	
A5145	HOOK, GARMENT, DOUBLE, SS	C.C.	4	EQUIP.	-	-	-	YES	NEW	PROVIDE BACKING IF IN BETWEEN STUDS	
A5200	DISPENSER, TOILET TISSUE, SS, 2-ROLL, SURFACE MOUNTED	C.C.	2	EQUIP.	-	-	-	-	NO	NEW	
A5220	BRACKET, TELEVISION, WALL, BACKING FOR O.R. WORKFLOW	V.V.	1	EQUIP.	-	-	-	YES	NEW	PROVIDE BACKING IF IN BETWEEN STUDS	
C0100	COUNTER, SOLID SURFACE	V.V.	1	FURN.	-	-	-	-	NO	NEW	COUNTER TO BE MOUNTED TO WALL STUDS
C0200	CABINET, U/C/B, 1 SHELF, 1 DRAWER, 1 DO, 36"x24"x22"	C.C.	3	FURN.	-	-	-	YES	NEW	PROVIDE BACKING	
CT020	COUNTERTOP, SOLID SURFACE	C.C.	1	FURN.	-	-	-	-	NO	NEW	
ED120	WORKSTATION, STRAIGHT, FREE STANDING, 60" W	V.V.	6	FURN.	-	A	-	-	NO	NEW	
ED124	WORKSTATION, STRAIGHT, FREE STANDING, 48" W	V.V.	3	FURN.	-	A	-	-	NO	NEW	
ED126	STAINLESS STEEL TABLE	V.V.	3	FURN.	-	-	-	-	NO	NEW	
F0275	CHAIR, SWIVEL, HIGH BACK	V.V.	9	FURN.	-	-	-	-	NO	NEW	
F0505	MOP BUCKET WITH WRINGER	V.V.	1	EQUIP.	-	-	-	-	NO	NEW	
F2010	BASKET, WASTEPAPER, STEP-ON	V.V.	2	FURN.	-	-	-	-	NO	NEW	
M1515	TELEVISION MONITORS, 10, 55" FOR O.R. WORK	V.V.	1	EQUIP.	-	A	-	-	NO	NEW	HOSPITAL GRADE, REQUIRE COEX, DATA
M1801	COMPUTER WITH FLAT PANEL MONITOR	V.V.	9	EQUIP.	-	A	-	-	NO	NEW	REQUIRE DATA
M1804	COMPUTER ON WHEEL WITH FLAT PANEL MONITOR	V.V.	5	EQUIP.	-	A	-	-	NO	NEW	REQUIRE DATA
M2080	SHELVING, STORAGE	V.V.	1	EQUIP.	-	-	-	-	NO	NEW	
M8920	VACUUM WET/DRY, HEPA FILTRATION	V.V.	1	EQUIP.	-	A	-	-	NO	NEW	
M8920	CART FOR CIDEXs 35 x 20 x 25	V.V.	2	EQUIP.	-	-	-	-	NO	NEW	MOVE THE EXISTING CIDEXs AND THEIR COMPONENTS TO THE NEW CART
M8930	CART FOR CIDEXs 20 x 30	V.V.	2	EQUIP.	-	-	-	-	NO	NEW	MOVE THE EXISTING CIDEXs AND THEIR COMPONENTS TO THE NEW CART
U5000	CLEANER, STEAM, MOBILE	V.V.	1	EQUIP.	-	F	-	-	NO	NEW	
U6000	AIRECORE CABINET	V.V.	1	EQUIP.	-	-	-	-	NO	NEW	
U7000	HIGH-PRESSURE WASHER	V.V.	1	EQUIP.	Y	A	-	-	NO	NEW	NEEDS TO CONNECT TO FAUCET W/ HOSE
U8000	BLOWER - DRYER	V.V.	1	EQUIP.	-	-	-	-	NO	NEW	
U9000	CONTROLLER FOR O.R. WORKFLOW	V.V.	1	EQUIP.	-	-	-	-	NO	NEW	REQUIRE DATA
1/A/2005	EXISTING 2-CELLS OMNICELES IN SPS MODULAR BUILDING 1 ROOM M-114	V.V.	2	EQUIP.	-	B	-	-	NO	EXIST	REQUIRE DATA FOR THE BRAIN REQUIRE SEISMIC STRAPPING
1/A/2005	EXISTING 3-CELLS OMNICELES IN SPS MODULAR BUILDING 1 ROOM M-114	V.V.	2	EQUIP.	-	B	-	-	NO	EXIST	REQUIRE DATA FOR THE BRAIN REQUIRE SEISMIC STRAPPING
1/A/2005	EXISTING UPPER AND LOWER CABINET IN SPS MODULAR BUILDING 1 ROOM M-114	V.V.	1	FURN.	-	-	-	YES	EXIST	REQUIRE FLOOR ANCHORS AND BACKING	
1/A/2005	EXISTING STETHOSCOPE CABINET IN SPS MODULAR BUILDING 1 ROOM M-114	V.V.	1	EQUIP.	-	A	-	-	YES	EXIST	PROVIDE BACKING
1/A/2005	EXISTING DRYING CABINET IN SPS MODULAR BUILDING 1 ROOM M-114	V.V.	1	EQUIP.	-	A	-	-	YES	EXIST	PROVIDE BACKING
1/A/2005	EXISTING CASE CARTS IN SPS MODULAR BUILDING 1 ROOM M-113	V.V.	3	EQUIP.	-	-	-	-	NO	EXIST	
1/A/2005	EXISTING STACKS OF SPS RED/ BLUE BINS IN SPS MODULAR BUILDING 1 ROOM M-114	V.V.	-	EQUIP.	-	-	-	-	NO	EXIST	QUANTITIES ARE UNKNOWN
1/A/2005	EXISTING 3-CELLS OMNICELES IN SPS MODULAR BUILDING 1 ROOM M-114	V.V.	1	EQUIP.	-	B	-	-	NO	EXIST	REQUIRE SEISMIC STRAPPING
1/A/2005	EXISTING LABEL PRINTER IN SPS MODULAR BUILDING 1 ROOM M-114	V.V.	1	EQUIP.	-	A	-	-	NO	EXIST	REQUIRE DATA
1/A/2005	EXISTING COMPUTER WORK STATION IN SPS MODULAR BUILDING 1 ROOM M-114	V.V.	1	EQUIP.	-	A	-	-	NO	EXIST	REQUIRE DATA
1/A/2005	EXISTING SCALE AND ITS MEASURE IN SPS MODULAR BUILDING 1 ROOM M-114	V.V.	1	EQUIP.	-	A	-	-	NO	EXIST	REQUIRE DATA
1/A/2005	EXISTING UPPER CABINET IN SPS MODULAR BUILDING 1 ROOM M-114	V.V.	1	FURN.	-	-	-	YES	EXIST	REQUIRE BACKING	
1/A/2005	EXISTING KEY-LOCK CABINET IN SPS MODULAR BUILDING 1 ROOM M-119	V.V.	1	EQUIP.	-	-	-	-	NO	EXIST	REQUIRE ANCHORS INSTALLATION TO WALL, MOUNTING HEIGHT: 48" A.F.F. TO TOP OF CABINET
1/A/2005	EXISTING STEAMERS IN SPS MODULAR BUILDING 1 ROOM M-102	V.V.	2	EQUIP.	-	A	-	-	NO	EXIST	SUPPLIED BY THE END USERS REQUIRES HOSES TO CONNECT TO NEARBY FAUCET
1/A/2005	EXISTING COMPUTER WORK STATION IN SPS MODULAR BUILDING 1 ROOM M-115	V.V.	4	EQUIP.	-	A	-	-	NO	EXIST	REQUIRE DATA
1/A/2005	EXISTING COMPUTER WORK STATION IN SPS MODULAR BUILDING 1 ROOM M-116	V.V.	1	EQUIP.	-	A	-	-	NO	EXIST	REQUIRE DATA
1/A/2005	EXISTING METRO RACKS IN SPS MODULAR CORRIDOR 102	V.V.	2	EQUIP.	-	-	-	-	NO	EXIST	
1/A/2005	EXISTING Huddle BOARD IN SPS MODULAR BUILDING 1 ROOM M-119	V.V.	1	EQUIP.	-	-	-	-	NO	EXIST	REQUIRE WALL ANCHORS MOUNTING HT: TBD
1/A/2005	EXISTING ERGONOMIC CHECK-IN TABLE IN SPS MODULAR BUILDING 1 ROOM M-114	V.V.	1	EQUIP.	-	A	-	-	NO	EXIST	SUPPLIED BY THE END USERS
1/A/2006	EXISTING CASE CARTS IN SPS MODULAR BUILDING 2	V.V.	60	EQUIP.	-	-	-	-	NO	EXIST	
1/A/2006	EXISTING WIRE CARTS IN SPS MODULAR BUILDING 2	V.V.	45	EQUIP.	-	-	-	-	NO	EXIST	
1/A/2006	EXISTING SPS METRO RACKS IN SPS MODULAR BUILDING 2	V.V.	70	EQUIP.	-	-	-	-	NO	EXIST	
1/A/2006	EXISTING 3-CELLS OMNICELES IN SPS MODULAR BUILDING 2	V.V.	12	EQUIP.	-	B	-	-	NO	EXIST	REQUIRE DATA FOR THE BRAIN REQUIRE SEISMIC STRAPPING
1/A/2006	EXISTING 2-CELLS OMNICELES IN SPS MODULAR BUILDING 2	V.V.	1	EQUIP.	-	B	-	-	NO	EXIST	REQUIRE DATA FOR THE BRAIN REQUIRE SEISMIC STRAPPING
1/A/2006	EXISTING CENITRAC COMPUTER WORKSTATION IN SPS MODULAR BUILDING 2	V.V.	2	EQUIP.	-	A	-	-	NO	EXIST	REQUIRE DATA
2/A/2006	EXISTING SCS PEGASUS RACKS IN SCS TEMP. TRAILER	V.V.	55	EQUIP.	-	-	-	-	NO	EXIST	
2/A/2006	EXISTING SCS CARTS IN SCS MAIN TEMP. TRAILER	V.V.	7	EQUIP.	-	-	-	-	NO	EXIST	QUANTITIES SUBJECT TO CHANGE
2/A/2006	EXISTING SCS TALL CABINETS IN STORAGE ROOM FB-360	V.V.	2	EQUIP.	-	-	-	-	NO	EXIST	
1/A/2007	EXISTING ETCHING MACHINE IN STORAGE ROOM FB-250	V.V.	1	EQUIP.	-	A	-	-	NO	EXIST	REQUIRE DATA EQUIPMENT CONSISTS OF: (2) COMPUTERS AND THEIR ACCESSORIES AND SUPPORTS (MONITOR ARMS); (2) RACKS; (2) DESK LIGHTS; (2) S.S. TABLES EQUIPMENT REQUIRE ASSEMBLY AFTER THE MOVE MONITOR ARM INSTALLATION REQUIRES ANCHORS
2/A/2007	EXISTING PREP & PACK COMPUTERS AND THEIR ACCESSORIES IN O.R. TEMP. STERIS TRAILER	V.V.	4	EQUIP.	-	A	-	-	NO	EXIST	REQUIRE DATA
3/A/2007	EXISTING PREP & PACK COMPUTERS AND THEIR ACCESSORIES IN EYE & DENTAL TEMP. STERIS TRAILER	V.V.	4	EQUIP.	-	A	-	-	NO	EXIST	REQUIRE DATA
3/A/2007	EXISTING DENTAL LUBRICATIONS & THEIR ACCESSORIES IN EYE & DENTAL TEMP. STERIS TRAILER	V.V.	2	EQUIP.	-	A	-	Y	-	NO	THEY NEED TO BE CONNECTED TO AIR TANK PUMP, DENTAL LUBRICATIONS REQUIRE AIR PRESSURE 0.5-0.6 MPa
3/A/2007	EXISTING DENTAL LUBRICATIONS' AIR TANK PUMP IN EYE & DENTAL TEMP. STERIS TRAILER	V.V.	1	EQUIP.	-	A	-	Y	-	NO	RUN A LINE TO CONNECT TO THE DENTAL LUBRICATIONS. LINE NEEDS TO BE SEISMICALLY SUPPORTED
2/A/2007	EXISTING COMPUTER AND ITS ACCESSORIES IN O.R. TEMP. STERIS TRAILER	V.V.	1	EQUIP.	-	A	-	-	NO	EXIST	REQUIRE DATA ALSO RELOCATE (E) MONITOR ARM IF APPLY MONITOR ARM INSTALLATION REQUIRES ANCHORS
3/A/2007	EXISTING COMPUTER AND ITS ACCESSORIES IN EYE & DENTAL TEMP. STERIS TRAILER	V.V.	1	EQUIP.	-	A	-	-	NO	EXIST	REQUIRE DATA ALSO RELOCATE (E) MONITOR ARM IF APPLY MONITOR ARM INSTALLATION REQUIRES ANCHORS

1 PHASE 1 EQUIPMENT AND FURNITURE SCHEDULE

EQUIPMENT AND FURNITURE SCHEDULE CONTINUED

MARK	TYPE	ACQ	QTY	FURN/ EQUIP.	Utilities			BACKING	STATUS (EXIST/ NEW)	REMARKS	
					Plumbing	Electrical	Misc Gas				
2/A/2007	EXISTING PREP & PACK MISC. EQUIPMENT IN O.R. TEMP. STERIS TRAILER	V.V.		EQUIP.	-	A	-	-	NO	EXIST	REQUIRE DATA FOR SOME EQUIPMENT CONSISTS OF: HAND-HELD SCANNERS; DOCUMENT SCANNERS; SEAL MACHINES LABEL PRINTERS, ETC.
3/A/2007	EXISTING PREP & PACK MISC. EQUIPMENT IN EYE & DENTAL TEMP. STERIS TRAILER	V.V.		EQUIP.	-	A	-	-	NO	EXIST	REQUIRE DATA FOR SOME EQUIPMENT CONSISTS OF: HAND-HELD SCANNERS; DOCUMENT SCANNERS; SEAL MACHINES LABEL PRINTERS, ETC.
2/A/2007	EXISTING CIDEXs AND THEIR ACCESSORIES IN O.R. TEMP. STERIS TRAILER	V.V.	2	EQUIP.	-	-	-	-	NO	EXIST	
3/A/2007	EXISTING CIDEXs AND THEIR ACCESSORIES IN EYE & DENTAL TEMP. STERIS TRAILER	V.V.	2	EQUIP.	-	-	-	-	NO	EXIST	
1/A/2007	EXISTING PURE ERGO. TABLE IN STORAGE ROOM FB-250	V.V.	1	EQUIP.	-	A	-	-	NO	EXIST	SUPPLIED BY THE END USERS
2/A/2007	EXISTING INSPEKTOR BORESCOPES AND THEIR ACCESSORIES IN O.R. TEMP. STERIS TRAILER	V.V.	2	EQUIP.	-	A	-	-	NO	EXIST	SUPPLIED BY THE END USERS REQUIRE DATA
2/A/2007	EXISTING INSPEKTOR BORESCOPES AND THEIR ACCESSORIES IN EYE & DENTAL TEMP. STERIS TRAILER	V.V.	2	EQUIP.	-	A	-	-	NO	EXIST	SUPPLIED BY THE END USERS REQUIRE DATA
2/A/2007	EXISTING COMPUTER AND ITS ACCESSORIES IN O.R. TEMP. STERIS TRAILER	V.V.	1	EQUIP.	-	A	-	-	NO	EXIST	REQUIRE DATA MOVE TO (E) COMPUTER ON WHEELS
3/A/2007	EXISTING COMPUTER AND ITS ACCESSORIES IN EYE & DENTAL TEMP. STERIS TRAILER	V.V.	1	EQUIP.	-	A	-	-	NO	EXIST	REQUIRE DATA MOVE TO (E) COMPUTER ON WHEELS
1/A/2008	EXISTING SCS 3-CELLS OMNICELES IN CLEAN LINEN STAGING ROOM GB-101	V.V.	1	EQUIP.	-	B	-	-	NO	EXIST	REQUIRE DATA FOR THE BRAIN
1/A/2008	EXISTING SCS UNDERCOUNTER REFRIGERATOR IN IT DEPLOYMENT STORAGE ROOM GB-103	V.V.	1	EQUIP.	-	A	-	-	NO	EXIST	
1/A/2008	EXISTING SCS PEGASUS RACKS INIT DEPLOYMENT STORAGE ROOM GB-103	V.V.	14	EQUIP.	-	-	-	-	NO	EXIST	
1/A/2008	EXISTING CRASH CARTS IN CLEAN LINEN STAGING ROOM GB-101	V.V.	14	EQUIP.	-	B	-	-	NO	EXIST	
1/A/2009	EXISTING SCS PEGASUS RACKS IN STORAGE ROOM FB-220	V.V.	9	EQUIP.	-	-	-	-	NO	EXIST	
1/A/2010	EXISTING SCS PEGASUS RACKS IN STORAGE ROOM FB-360	V.V.	53	EQUIP.	-	-	-	-	NO	EXIST	
1/A/2010	EXISTING 3-CELLS OMNICELES IN STORAGE ROOM FB-360	V.V.	8	EQUIP.	-	-	-	-	NO	EXIST	
1/A/2010	EXISTING CRASH CARTS IN STORAGE ROOM FB-360	V.V.	5	EQUIP.	-	-	-	-	NO	EXIST	
1/A/2010	EXISTING COMPUTER ON WHEEL IN STORAGE ROOM FB-360	V.V.	1	EQUIP.	-	-	-	-	NO	EXIST	
1/A/2010	EXISTING SCS METRO CARTS IN STORAGE ROOM FB-360	V.V.	3	EQUIP.	-	-	-	-	NO	EXIST	
1/A/2010											
1/A/2010											
1/A/2010											

UTILITIES LEGEND:

- A 120 VOLT, CONVENTIONAL OUTLET
- B 120 VOLT, SPECIAL OUTLET (EMERGENCY OUTLET)
- F SPECIAL ELECTRICAL REQUIREMENTS
- G 208/ 220 VOLT, 3 PHASE

Office of Facility Planning and Development

VA

Project Title
VA Palo Alto - SPS/ SCS Renovation

City of Palo Alto
Santa Clara County, CA
Building Number
100
Project Number:
640-23-108

SHEET NOTES

FF&E PLAN
PHASE I

Revision:	Issue Date
END-USERS SIGN-OFF	05/09/2025
BACKCHECK 1	09/30/2025

Drawing Title:
Phase 1 Equipment & Furniture Schedule

Reference To:

Scale:
SEE DWG.
Date:
05/09/25

Drawing Number:
VA-011