



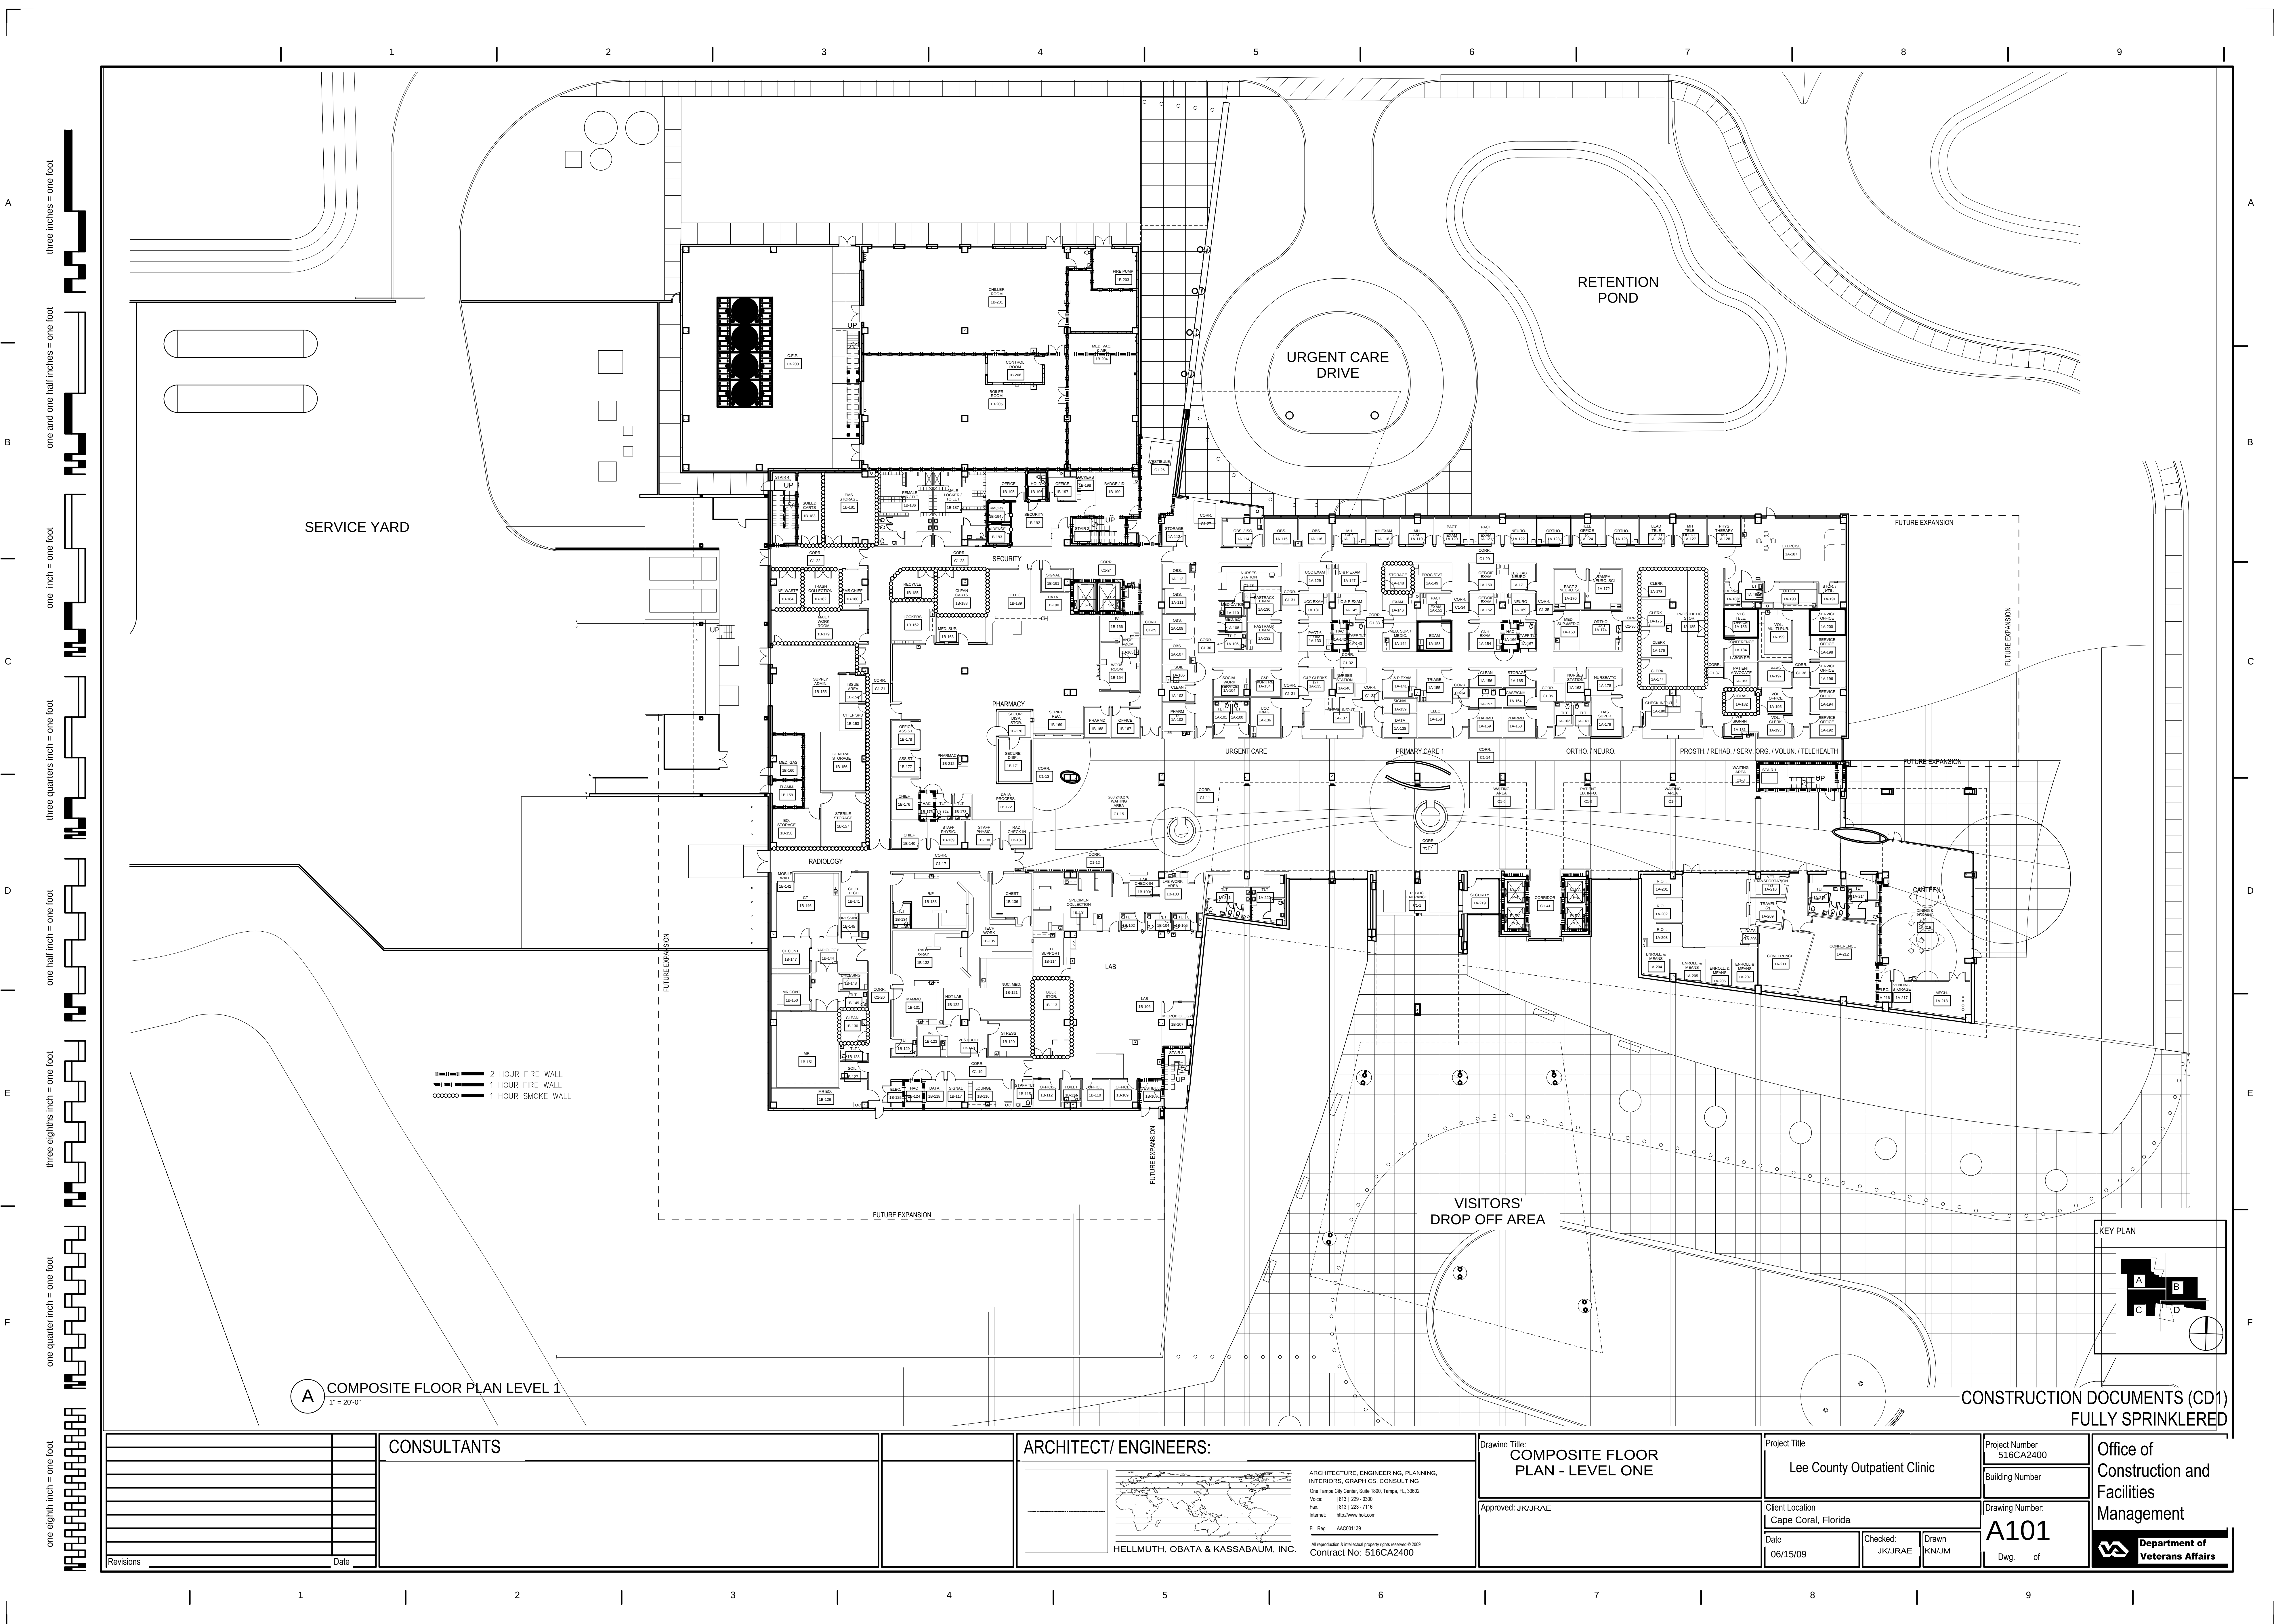


A COMPOSITE FLOOR PLAN LEVEL 1
1" = 20'-0"

2 HOUR FIRE WALL
1 HOUR FIRE WALL
1 HOUR SMOKE WALL

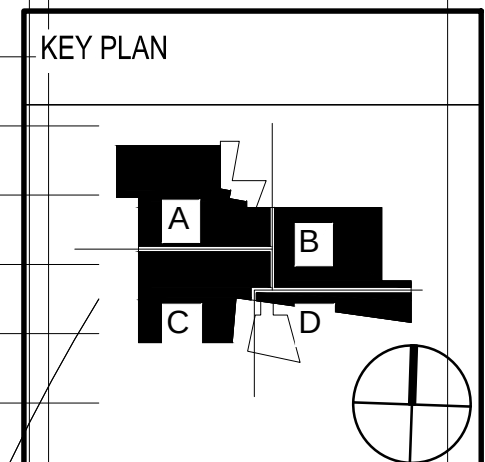

CONSTRUCTION DOCUMENTS (CD1)
FULLY SPRINKLERED

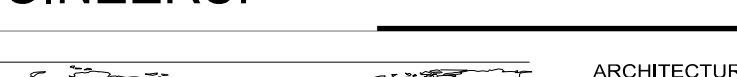				CONSULTANTS				ARCHITECT/ ENGINEERS:		Drawing Title: COMPOSITE FLOOR PLAN - LEVEL ONE		Project Title Lee County Outpatient Clinic		Project Number 516CA2400		Office of Construction and Facilities Management			
								 HELLMUTH, OBATA & KASSABAUM, INC.		ARCHITECTURE, ENGINEERING, PLANNING, INTERIORS, GRAPHICS, CONSULTING One Tampa City Center, Suite 1800, Tampa, FL 33602 Voice: (813) 223-1000 Fax: (813) 223-7116 Internet: http://www.hok.com FL Reg. AAC001159		Building Number		Drawing Number: A101					
						Approved: JK/JRAE						Client Location Cape Coral, Florida		Checked: JK/JRAE				Drawn KN/JM	
Revisions		Date										Date 06/15/09						Dwg. of	

Department of Veterans Affairs	
-----------------------------------	--

ARCHITECT/ ENGINEERS:

HELLMUTH, OBATA & KASSABAUM, INC.

ARCHITECTURE, ENGINEERING, PLANNING,
INTERIORS, GRAPHICS, CONSULTING
One Tampa City Center, Suite 1800, Tampa, FL 33602
Voice: (813) 229-0300
Fax: (813) 223-7116
Internet: <http://www.hok.com>
FL Reg. A6030159
All reproduction & intellectual property rights reserved © 2009
Contract No: 516CA2400

Project Title
Lee County Outpatient Clinic

Client Location
Cape Coral, Florida

Date
06/15/09

Checked:
JK/JRAE

Drawn
KN/JM

Dwg. of

Project Number
516CA2400

Building Number

Drawing Number:
A101

Dwg. of

A

B

C

D

E

F

A

B

C

D

E

F

three inches = one foot

one and one half inches = one foot

one inch = one foot

three quarters inch = one foot

one half inch = one foot

three eighths inch = one foot

one quarter inch = one foot


one eighth inch = one foot





A COMPOSITE FLOOR PLAN LEVEL 2
1" = 20'-0"

CONSTRUCTION DOCUMENTS (CD1)
FULLY SPRINKLERED

--	--	

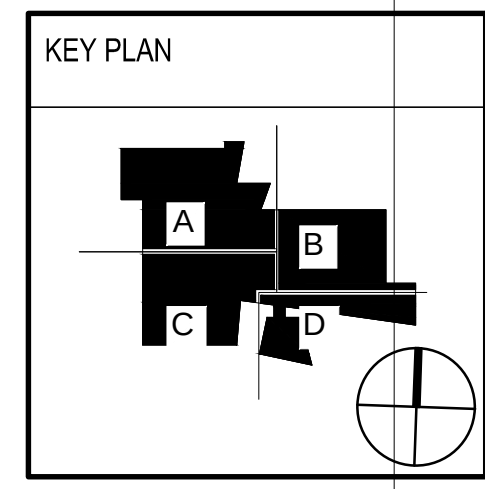

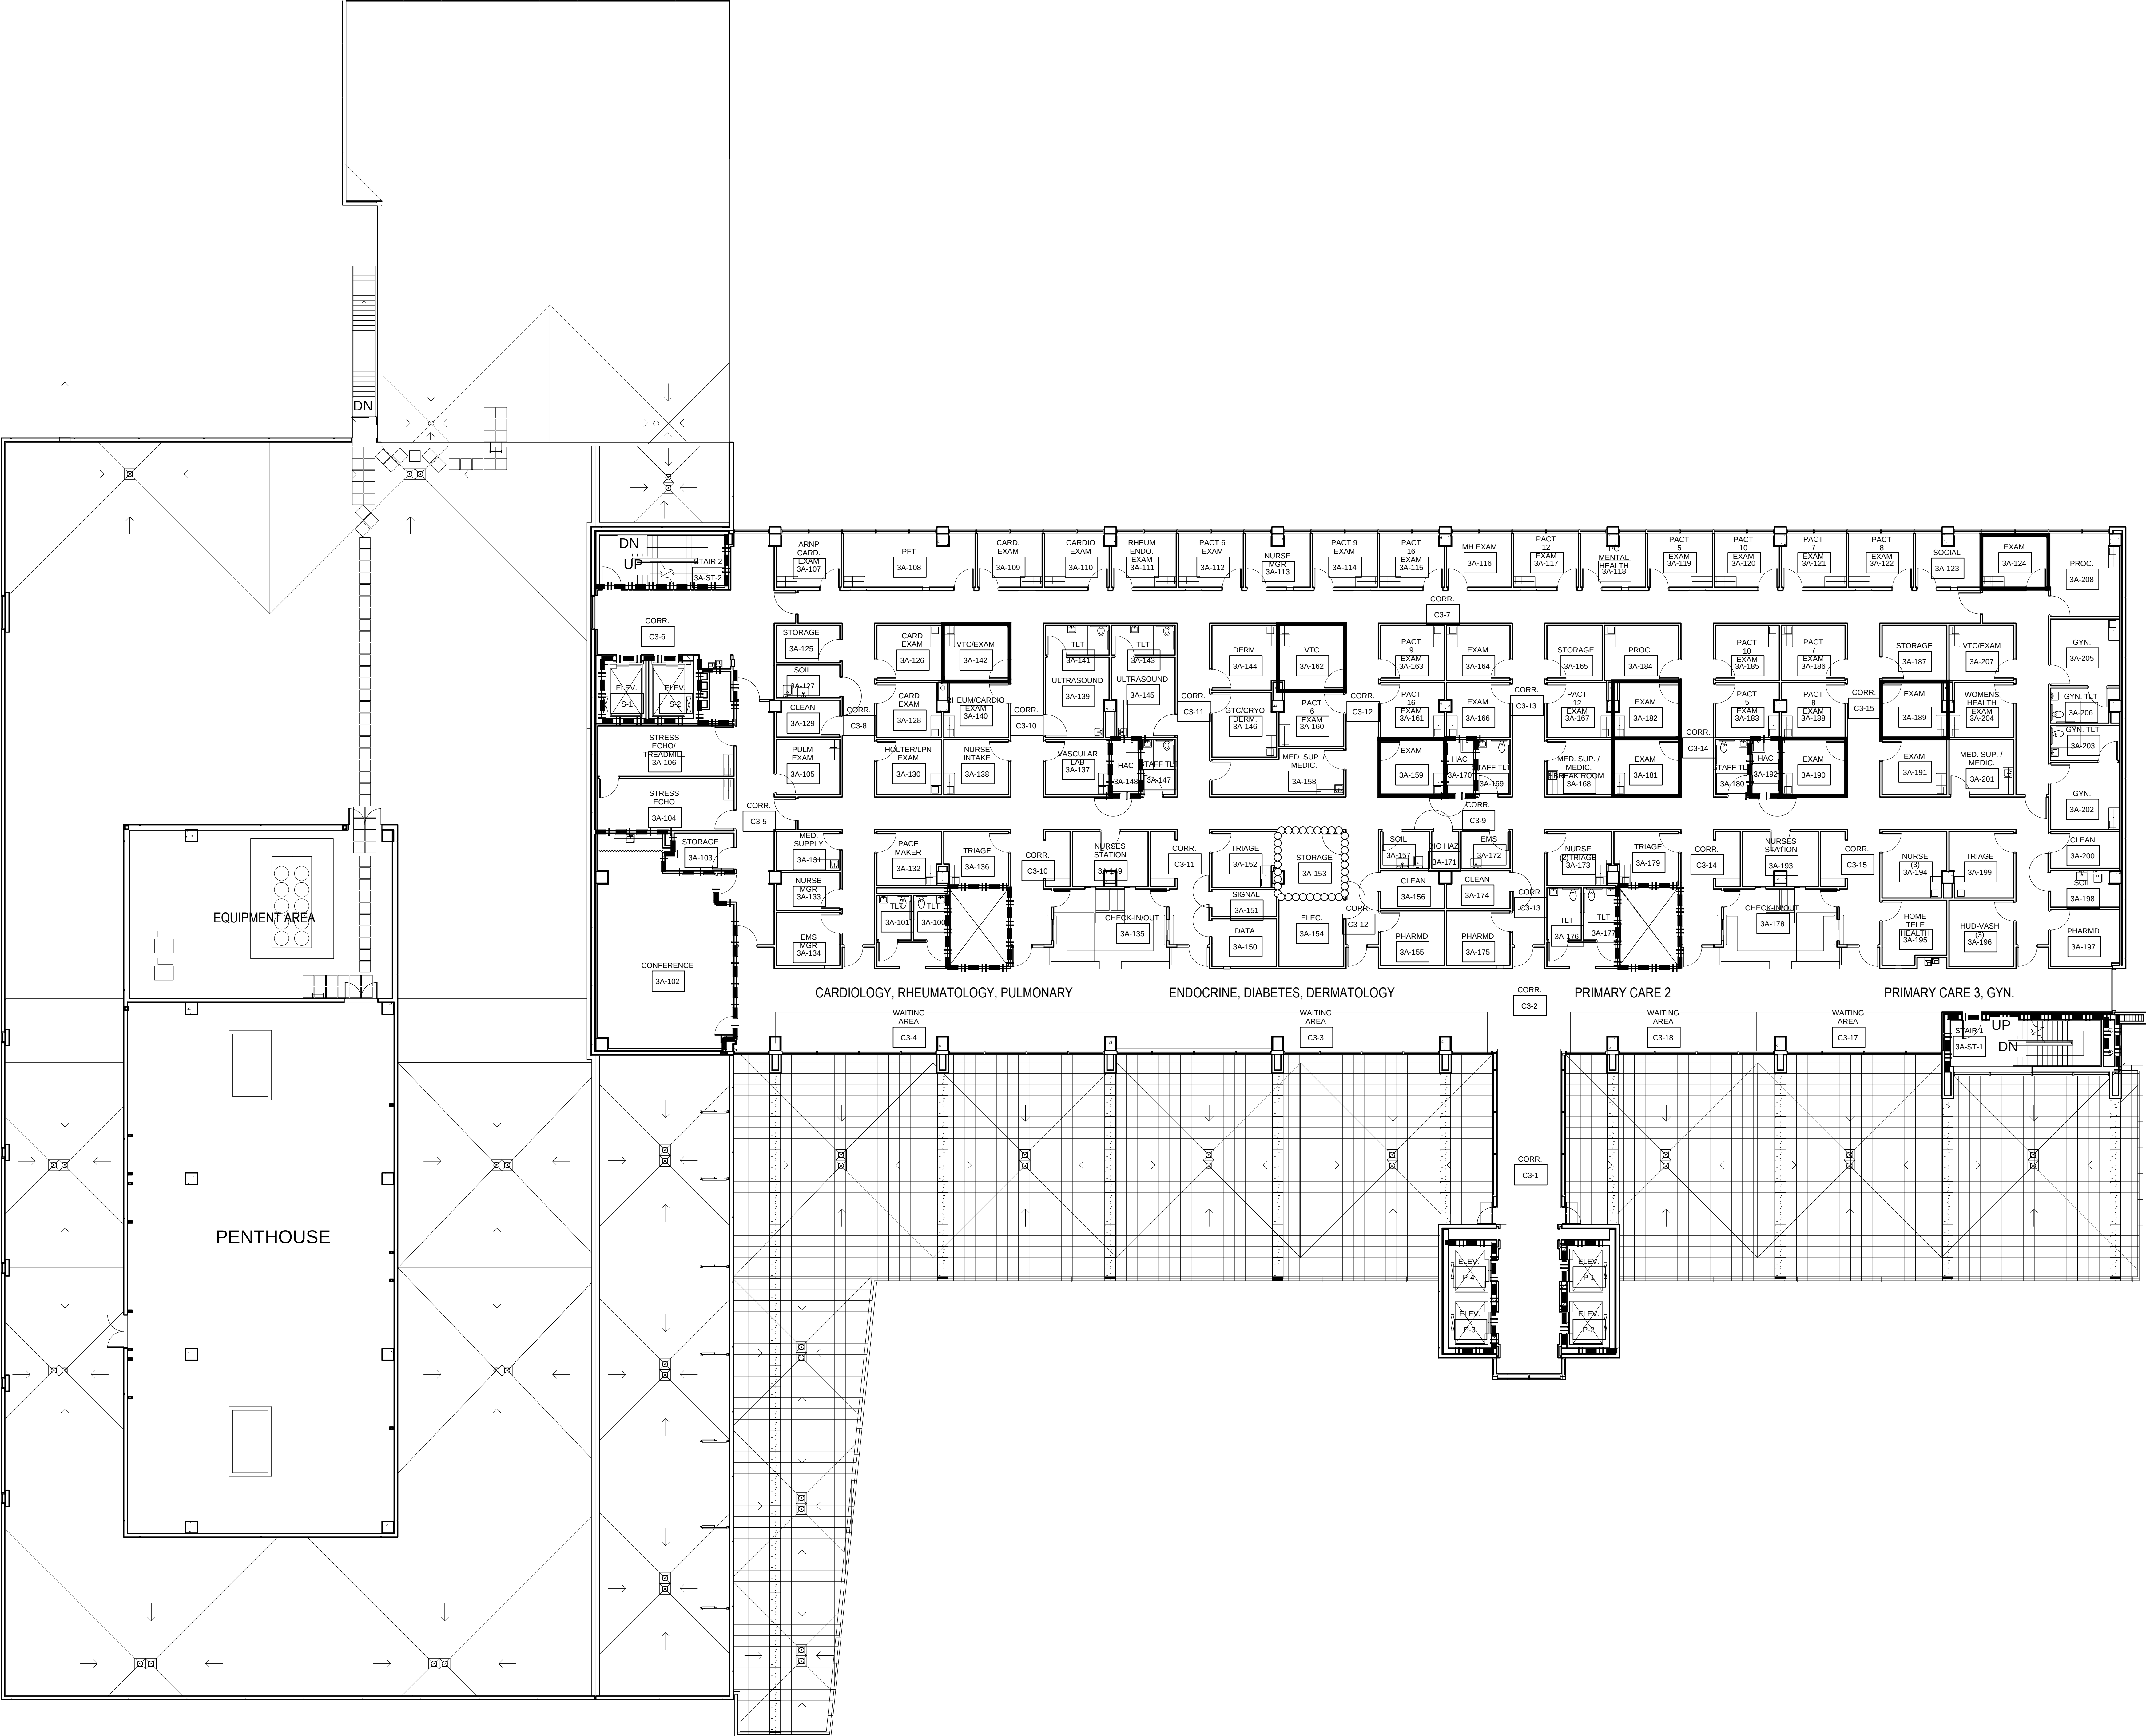

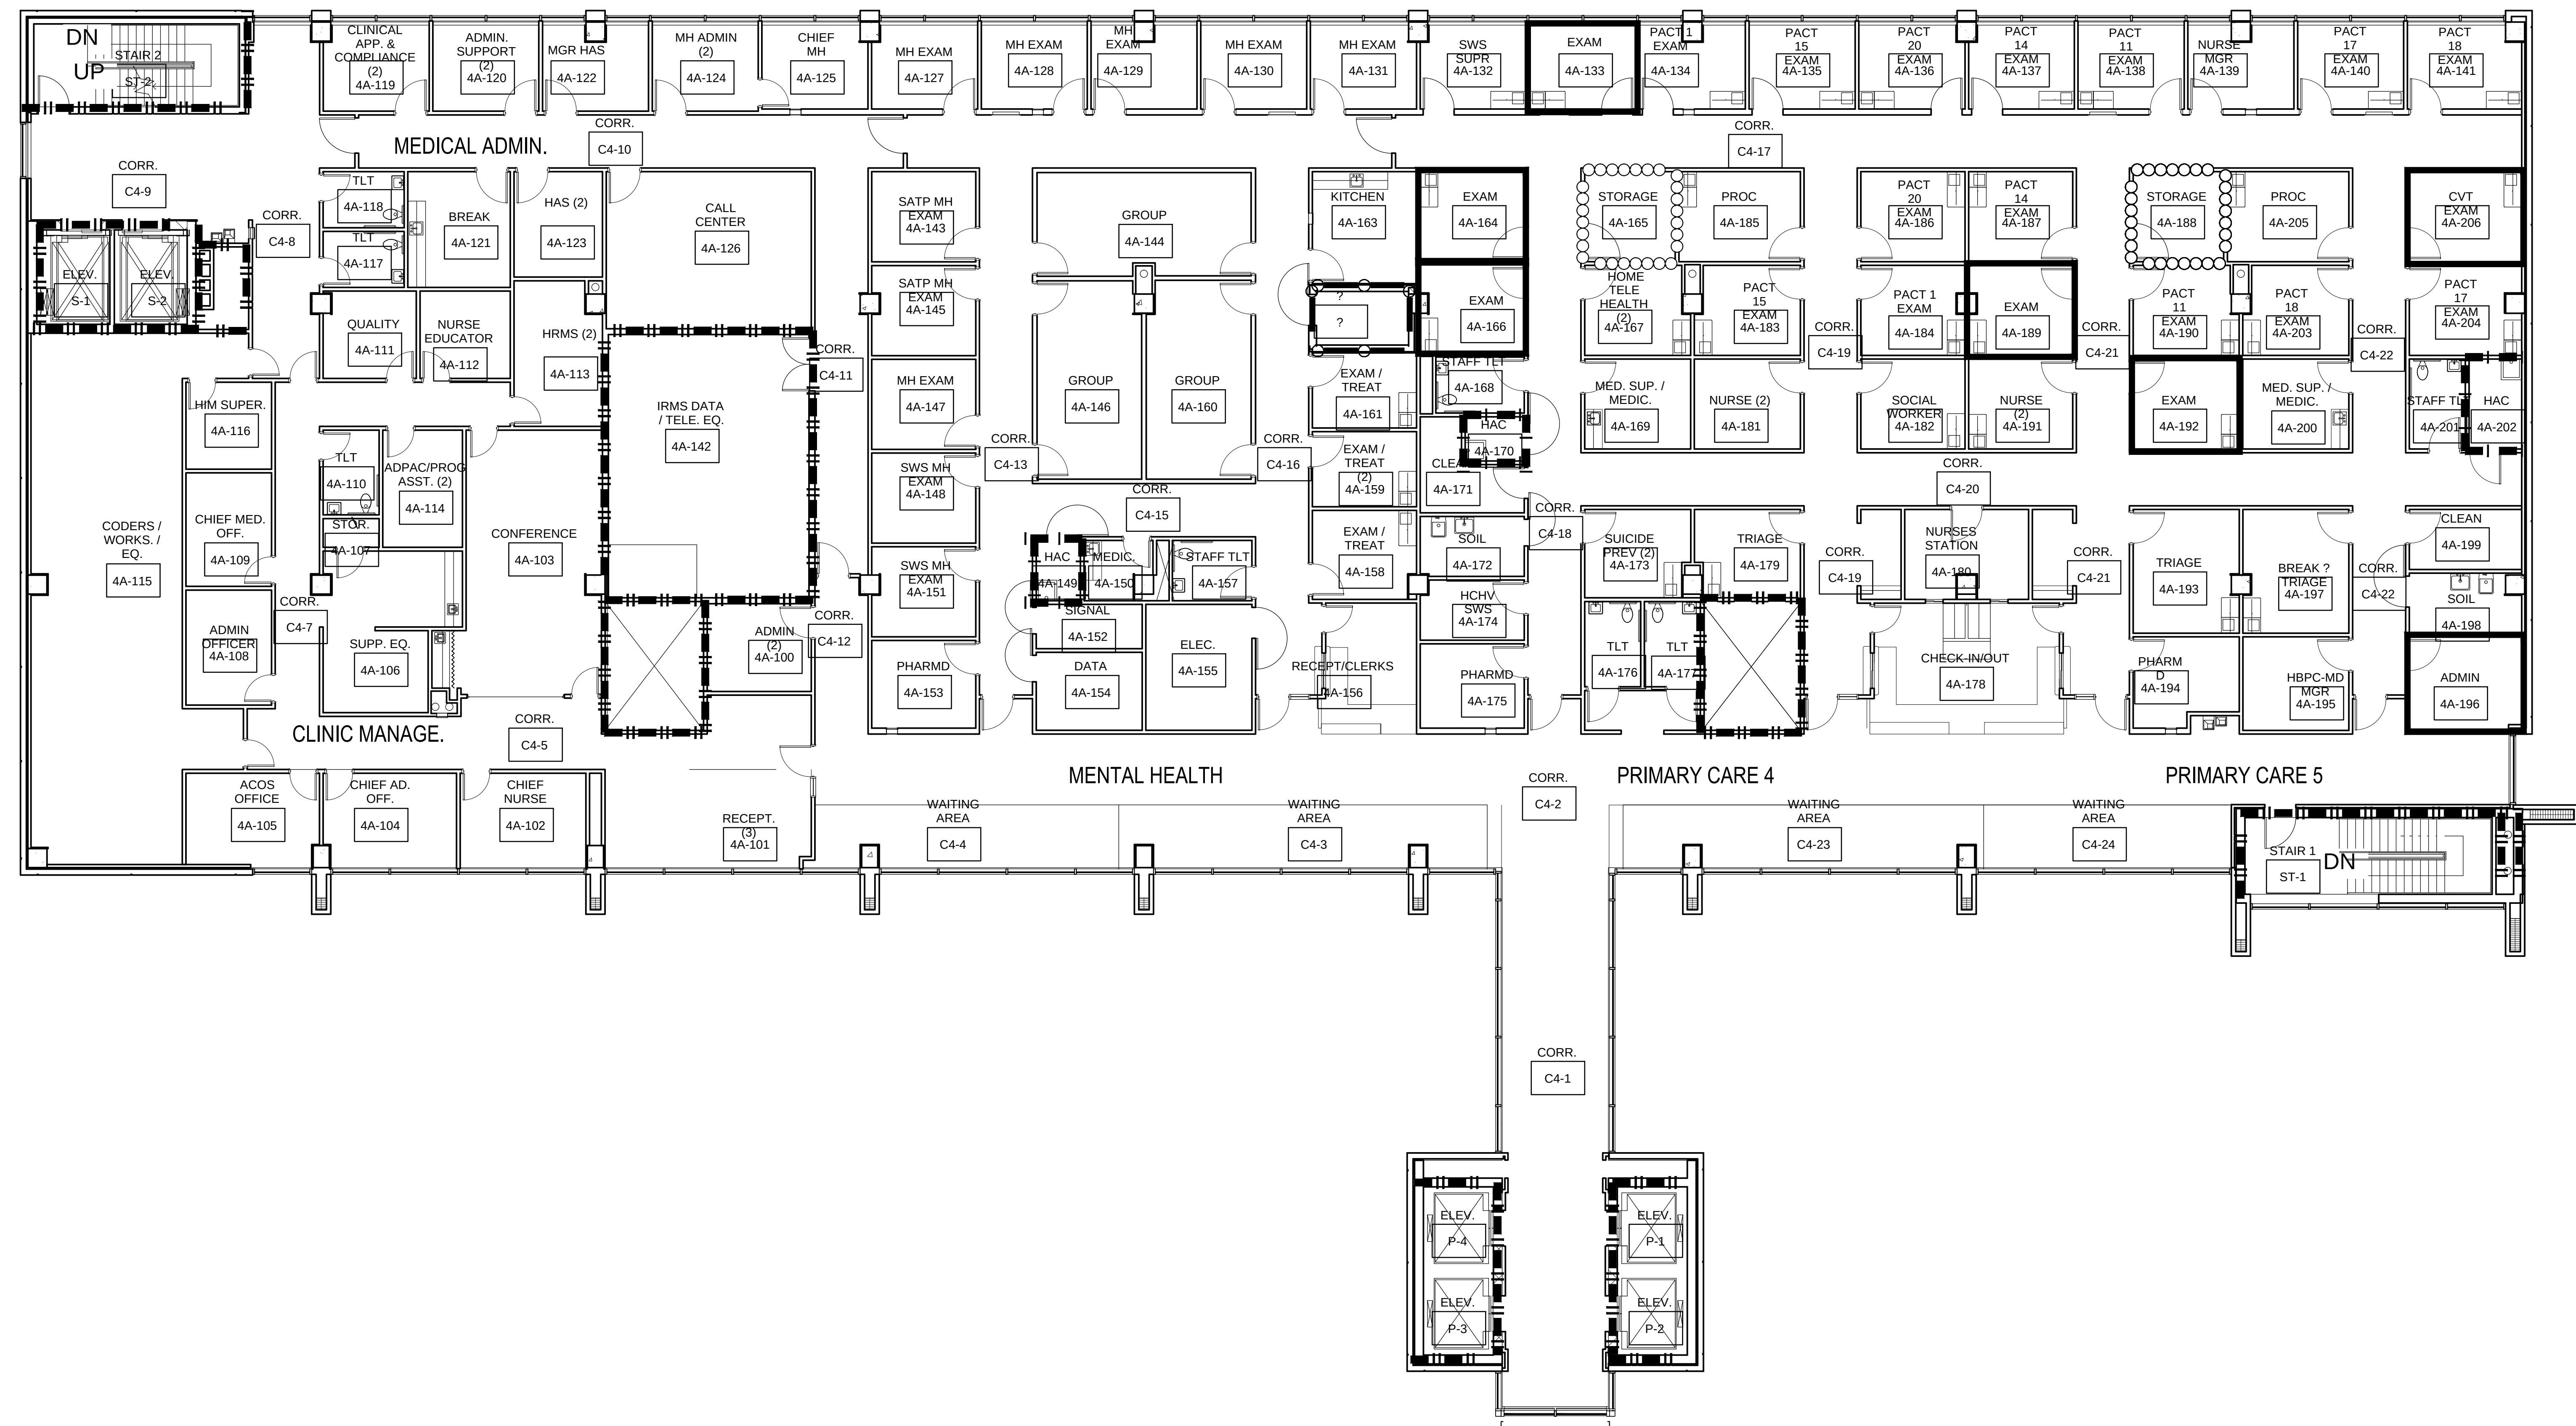

SUITE DESCRIPTIONS				
SUITE NUMBER	SUITE NAME	SUITE SIZE	TYPE OF SUITE	EXIT NUMBER
1	DENTAL SUITE	5,978 Sq. Ft.	NON SLEEPING PATIENT CARE	4
2	SAME DAY SURGERY SUITE	9,650 Sq. Ft.	NON SLEEPING PATIENT CARE	6

KEY NOTES:

- A** NON-FIRE-RATED SMOKE PARTITION.
- B** TWO STORY COMMUNICATING SPACE PER SECTION 8.6.6 OF NFPA 101-2018 EDITION.
- C** RATING PLATE VERIFIED UNDER PLANO HINGE.
- D** WINDOW SPRINKLER PROTECTION.
- E** ELECTRICAL TRANSFORMER ROOM CONSTRUCTED WITHOUT FIRE RATING. CONSTRUCTION WAS PRIOR TO THE CURRENT 1 HOUR REQUIREMENT NOW FOUND IN ARTICLE 430-21(b) OF NFPA 70 AND FIRST ADOPTED IN THE 1999 EDITION.

PARTITION LEGEND

- | | |
|---|--|
|  | HEALTH CARE OCCUPANCY CORRIDORS |
|  | SMOKE RESISTANT HAZARDOUS ROOM ENCLOSURE |
|  | NON-RATED SMOKE PARTITION |
|  | 1 HOUR FIRE BARRIER (HAZARDOUS ROOM ENCLOSURE) |
|  | SMOKE ZONE BARRIER |
|  | 2 HOUR FIRE BARRIER |
|  | 2 HOUR FIRE/SMOKE ZONE BARRIER |
|  | SUITE DESIGNATION |

SYMBOLS LIST

- | | |
|--|---|
| | HORIZONTAL EXIT PASSAGEWAY |
| | EXIT |
| | EXIT PASSAGEWAY |
| | LINEN CHUTE |
| | TRASH CHUTE |
| | AREA OPEN TO CORRIDOR – WITH SMOKE DETECTION |
| | AREA OPEN TO CORRIDOR – NO SMOKE DETECTION REQUIRED |
| | FIRE EXTINGUISHER |
| | EXIT SIGN |
| | EMERGENCY LIGHT |
| | FIRE ALARM STATION |
| | FIRE ALARM CONTROL PANEL |
| | FIRE ALARM ANNUNCIATOR PANEL |
| | AUTOMATED EXTERNAL DEFIBRILLATOR |
| | EYEWASH STATION |
| | SPRINKLER SYSTEM RISER |
| | SHOWER STATION |
| | EVACUATION CHAIR |
| | FIRE HOSE VALVE |



LEE COUNTY OPC BUILDING
SECOND FLOOR
FULLY SPRINKLERED
MIXED OCCUPANCY

FP & C Project Number:	1822.18	
75% DESIGN	Date: 11/04/18	
35% DESIGN	Date: 09/24/18	
Revisions:	Date:	
 FIRE PROTECTION & CODE CONSULTANTS, LLC 1250 MAIN STREET INDIANAPOLIS, IN 46224 317-996-1500		
CONSULTANT		
ARCHITECT/ENGINEER OF RECORD		
STAMP		
 5900 MEANS STREET NW ALF, NV, NV 89118 702-799-1500 Office of Construction and Facilities Management		
VA U.S. Department of Veterans Affairs		
Drawing Title		
LEE COUNTY BUILDING SECOND FLOOR		
Phase		
75% DESIGN		
Project Title		
FIRE AND LIFE SAFETY SURVEY		
Location		
VAMC BAY PINES, FL		
Issue Date	Checked	Drawn
11/04/2018	FVO	TK
Drawing Number		
Building Number		
LEE COUNTY		
Soc-2		

SUITE NUMBER	SUITE NAME	SUITE SIZE	TYPE OF SUITE	EXIT NUMBER
1	EXECUTIVE SUITE	4,375 Sq. Ft.	NON PATIENT CARE	3

SUITE DESCRIPTIONS

KEY NOTES:

- A

NON FIRE-RATED SMOKE PARTITION.
- B

FIRE SPRINKLERS INSTALLED PER FLOOR MOUNTED OBSTRUCTION SPACING REQUIREMENTS OF TABLE 8.6.5.2.2 IN NFPA 13-2013 EDITION.

PARTITION LEGEND

- HEALTH CARE OCCUPANCY CORRIDORS
- SMOKE RESISTIVE HAZARDOUS ROOM ENCLOSURE
- NON-RATED SMOKE PARTITION
- 1 HOUR FIRE BARRIER (HAZARDOUS ROOM ENCLOSURE)
- SMOKE ZONE BARRIER
- 2 HOUR FIRE BARRIER
- 2 HOUR FIRE/SMOKE ZONE BARRIER
- SUITE DESIGNATION

SYMBOLS LIST

- HORIZONTAL EXIT PASSAGEWAY
- EXIT
- EXIT PASSAGEWAY
- LINEN CHUTE
- TRASH CHUTE
- AREA OPEN TO CORRIDOR – WITH SMOKE DETECTION
- AREA OPEN TO CORRIDOR – NO SMOKE DETECTION REQUIRED
- FIRE EXTINGUISHER
- EXIT SIGN
- EMERGENCY LIGHT
- FIRE ALARM STATION
- FIRE ALARM CONTROL PANEL
- FIRE ALARM ANNUNCIATOR PANEL
- AUTOMATED EXTERNAL DETRIBRILLATOR
- EYEWASH STATION
- SPRINKLER SYSTEM RISER
- SHOWER STATION
- EVAQUATION CHAIR
- FIRE HOSE VALVE

FP & C Project Number: 1822.18

75% DESIGN	Date: 11/04/18
50% DESIGN	Date: 09/24/18
Revisions:	Date:

CONSULTANT



FIRE PROTECTION & CODE CONSULTANTS, LLC
INDIANAPOLIS, IN 46224
(317) 986-5188

ARCHITECT/ENGINEER OF RECORD



TOLAND MIZELL MOLNAR
590 MEANS STREET NW
SUITE 300
ATLANTA, GA 30318

STAMP

Office of Construction and Facilities Management

U.S. Department of Veterans Affairs

Drawing Title

LEE COUNTY BUILDING FOURTH FLOOR

Phase

75% DESIGN

Project Title

FIRE AND LIFE SAFETY SURVEY

Project Number


1822.18

Building Number


LEE COUNTY

Drawing Number

SOC-4


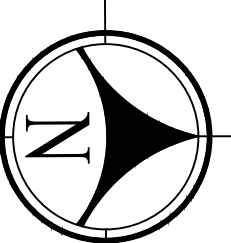


LEE COUNTY BUILDING
FOURTH FLOOR
FULLY SPRINKLERED
BUSINESS OCCUPANCY

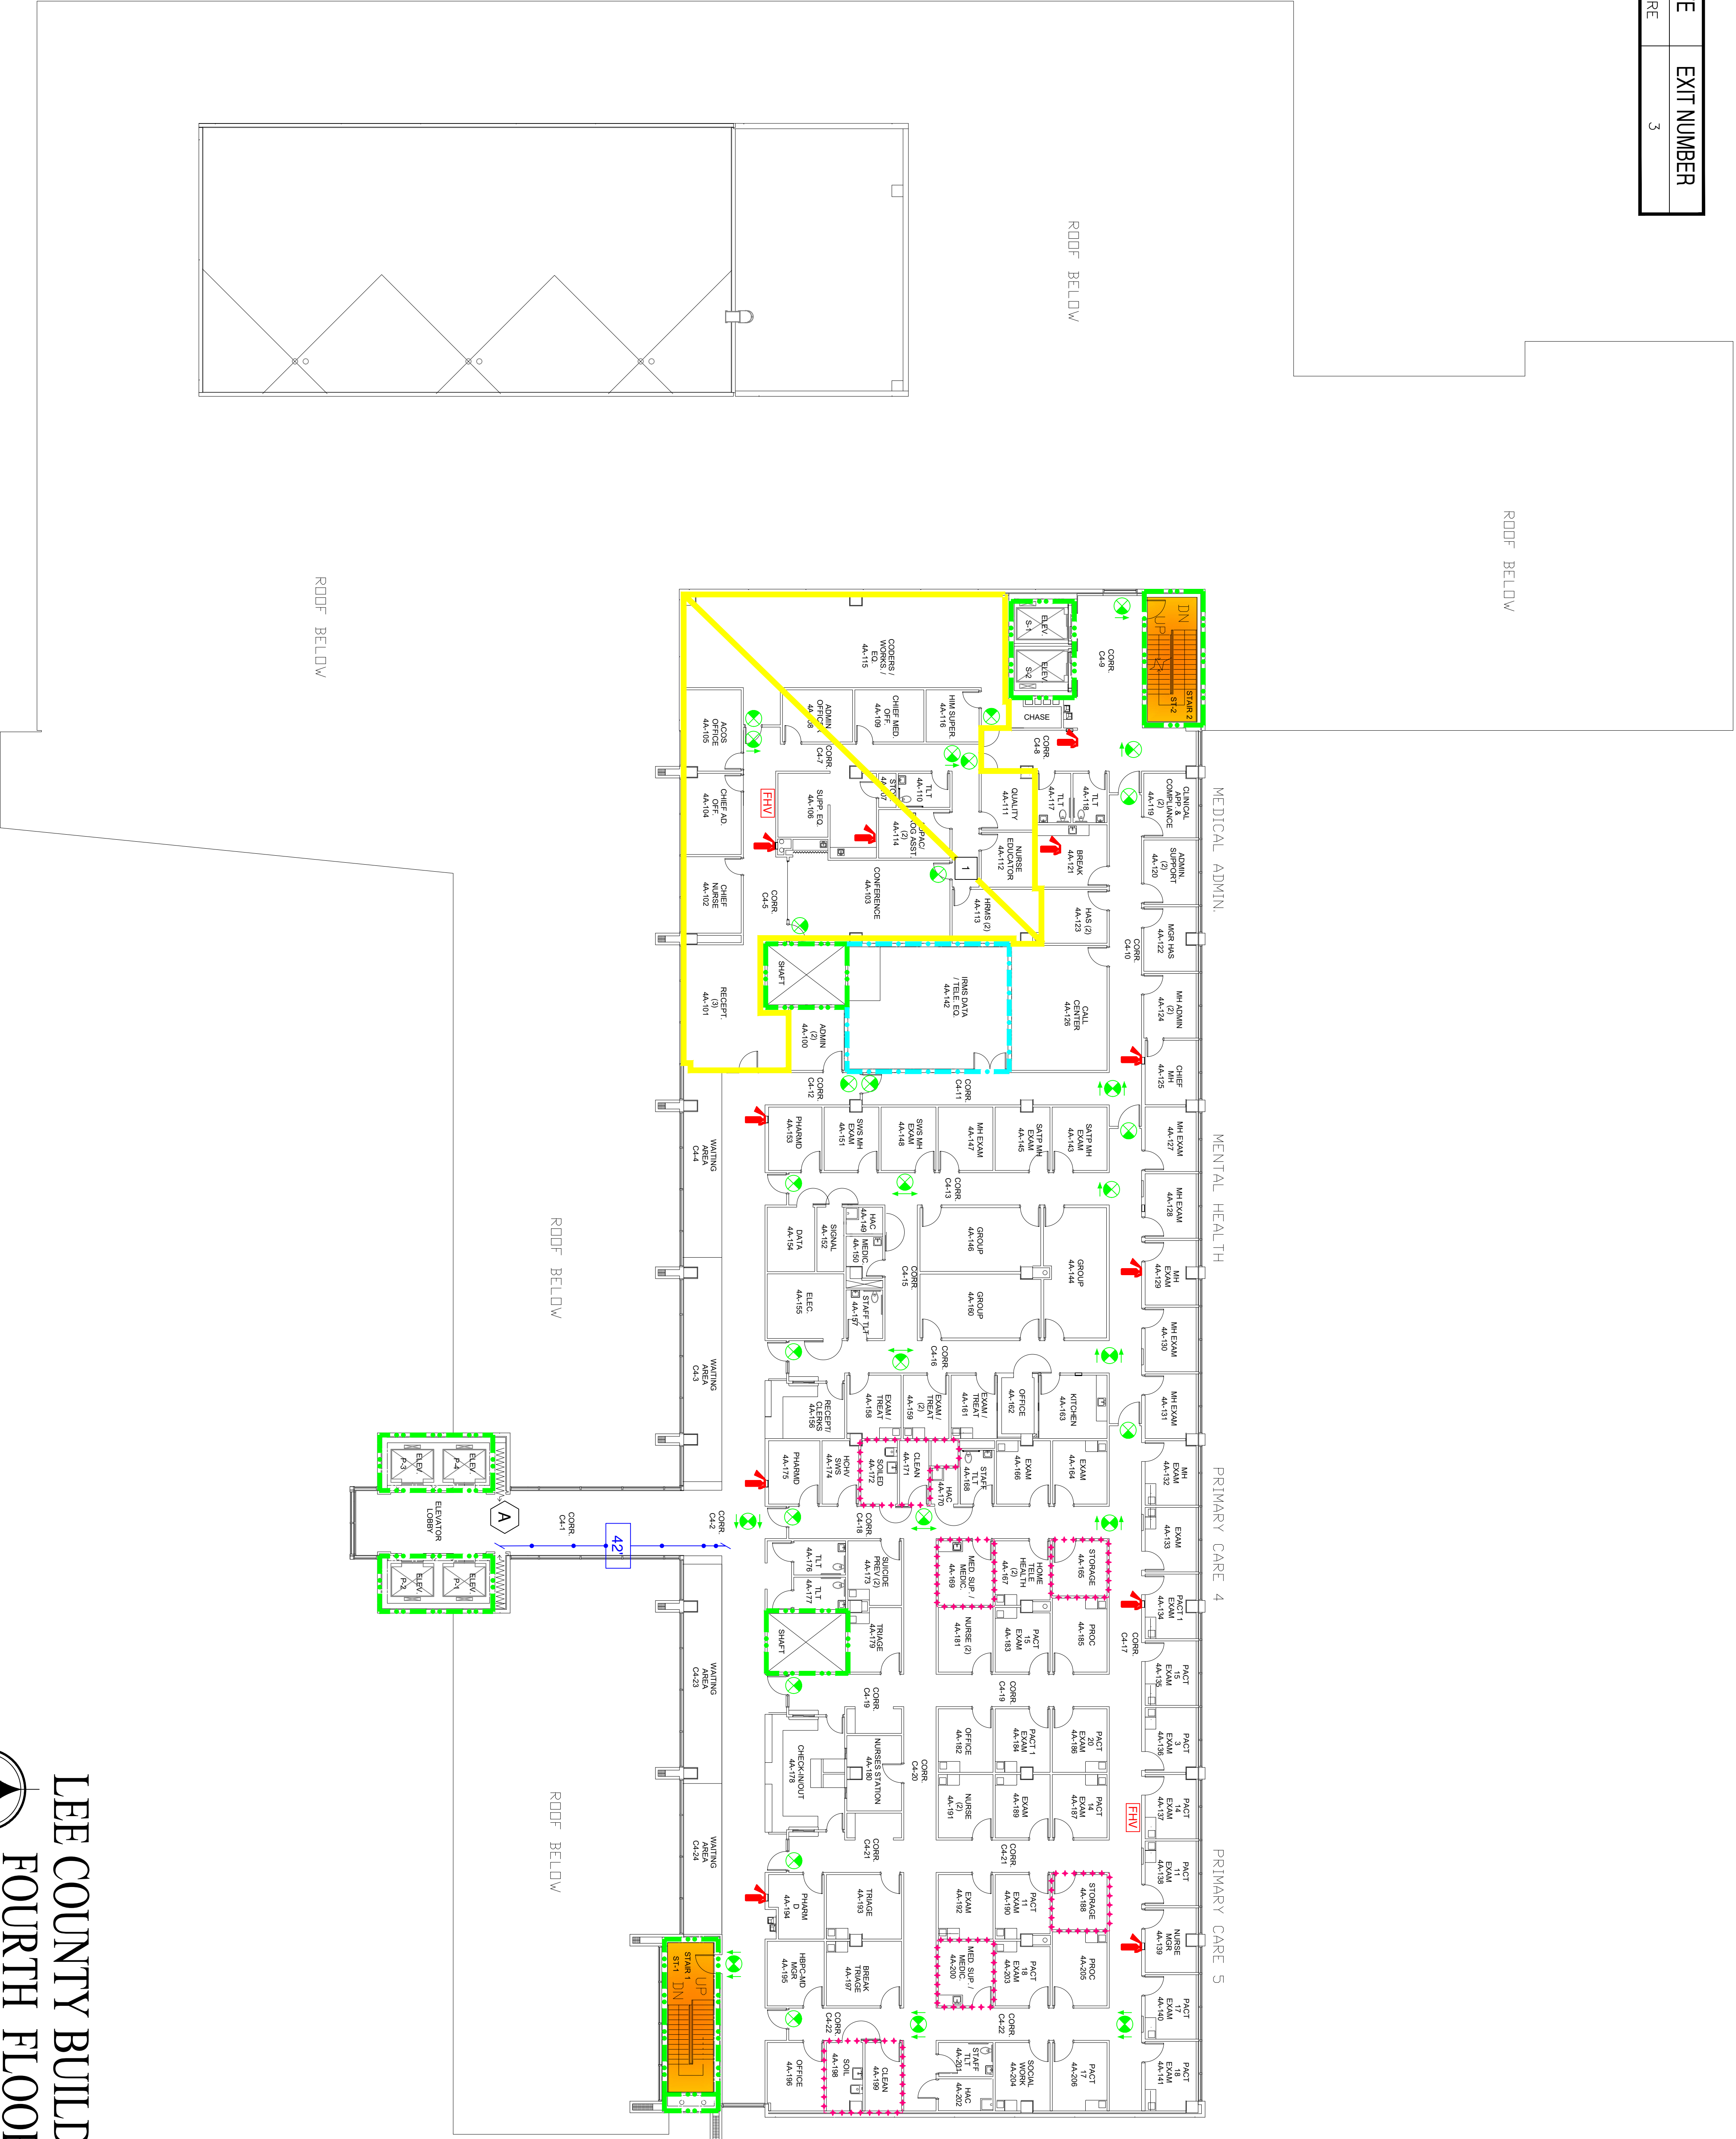


KEY NOTES:

A MECHANICAL ROOM PART OF SHAFT.

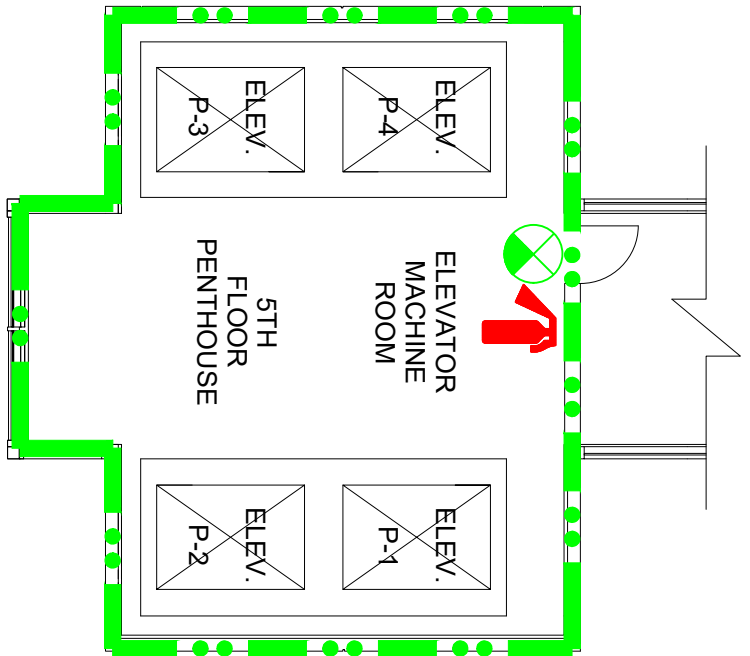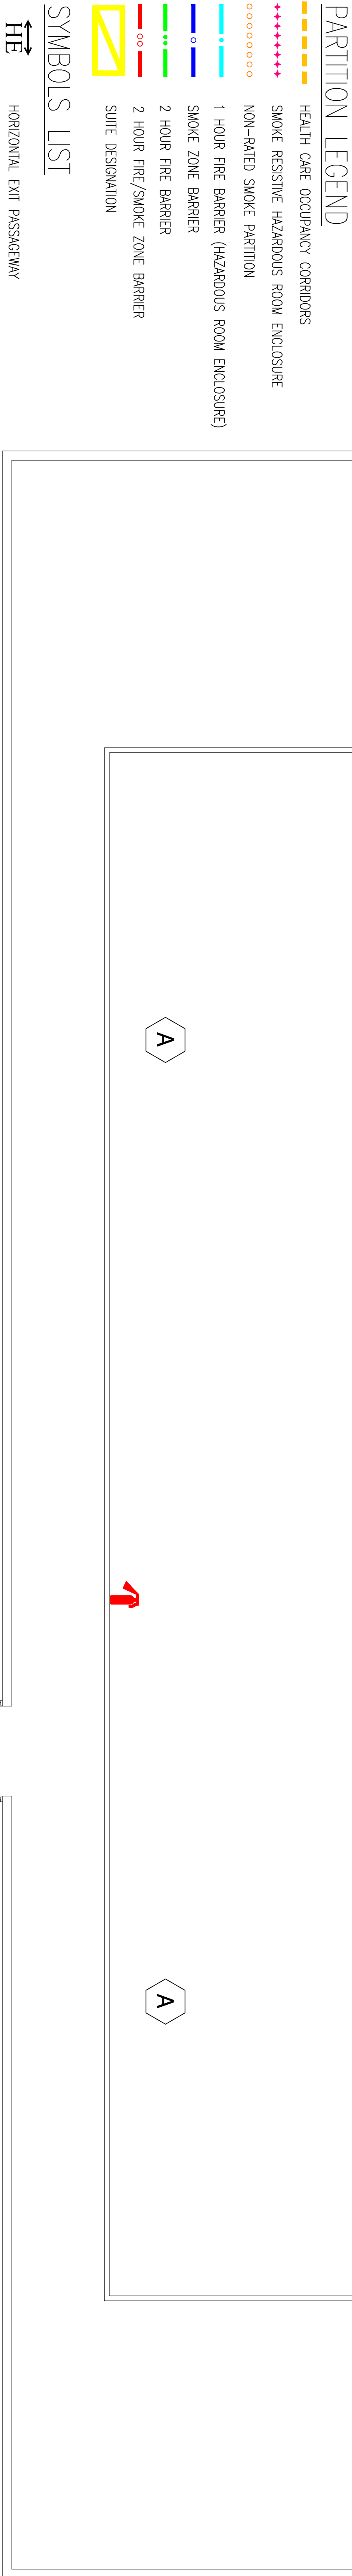

LEE COUNTY BUILDING
FIFTH FLOOR
FULLY SPRINKLERED
INDUSTRIAL OCCUPANCY

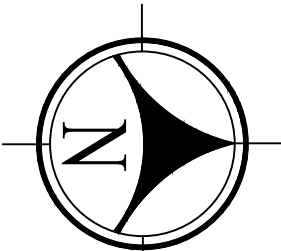

FP & C Project Number: 1822.18		CONSULTANT		ARCHITECT/ENGINEER OF RECORD		STAMP		Office of Construction and Facilities Management		Drawing Title LEE COUNTY BUILDING FIFTH FLOOR		Phase 75% DESIGN		Project Title FIRE AND LIFE SAFETY SURVEY		Building Number LEE COUNTY	
T&E DESIGN		DATE: 11/04/18		TOLAND MIZELL		500 MEANS STREET NW SUITE 300 ATLANTA, GA 30318		U.S. Department of Veterans Affairs		Approved: Project Director		FULLY SPRINKLERED		Location VAMC BAY PINES, FL		Drawing Number SOC-5	
SEA DESIGN		DATE: 09/24/18		FIRE PROTECTION & CODE CONSULTANTS										Issue Date 11/04/2018			
Revisions:		Date:												Checked PVO		Drawn TK	