
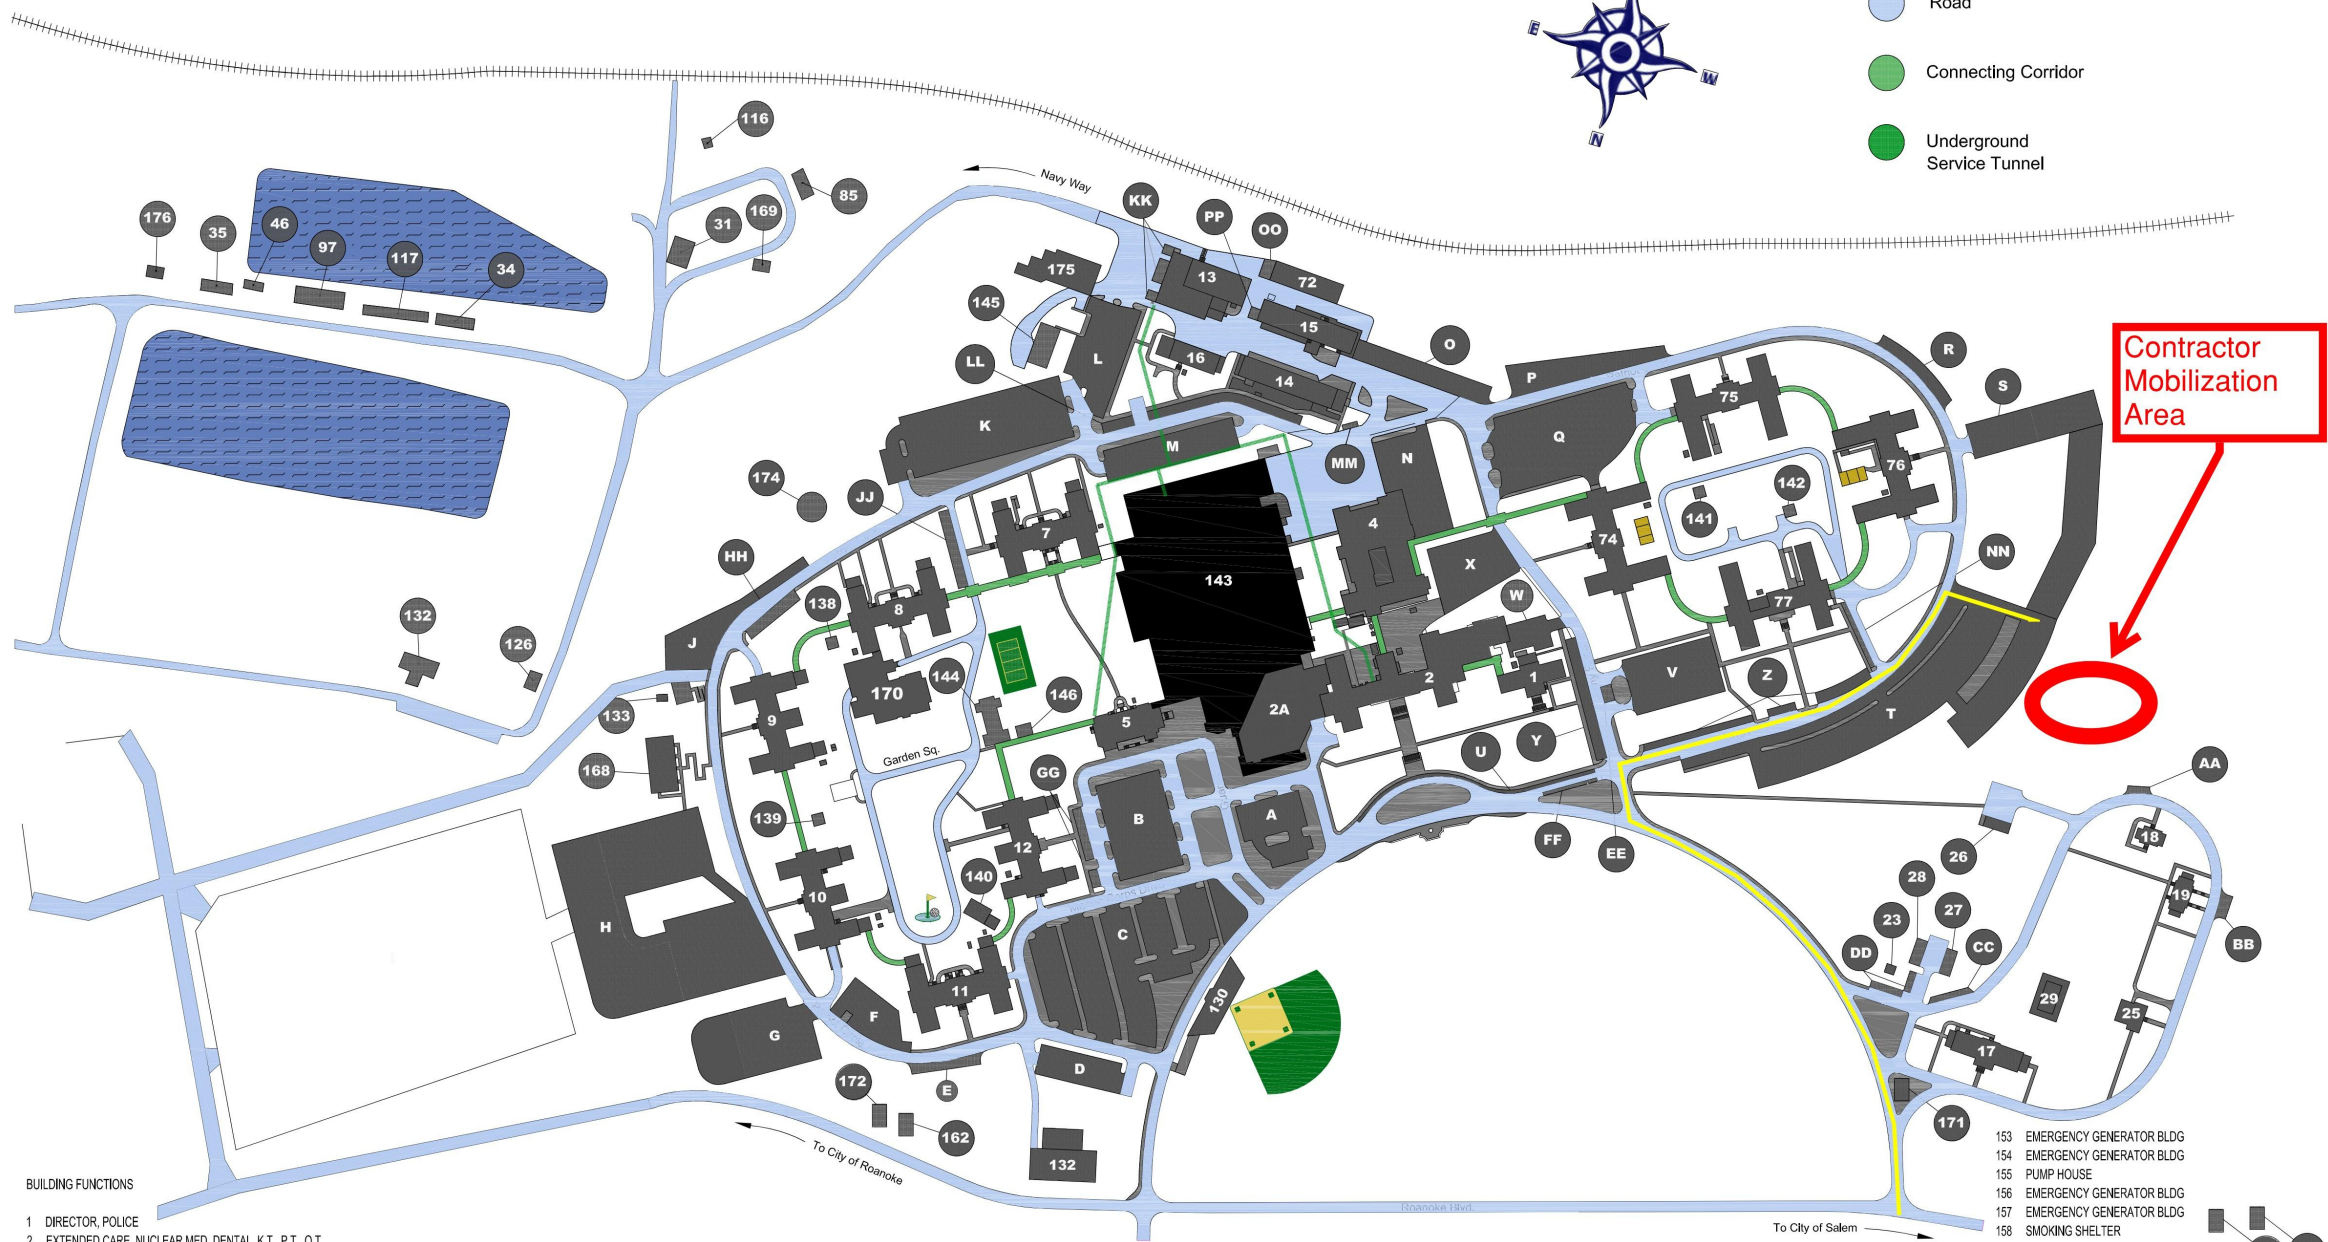


V.A. MEDICAL CENTER
SALEM, VA
FACILITY MAP

no scale

- T Parking Lot
- 143 Building
- Road
- Connecting Corridor
- Underground Service Tunnel

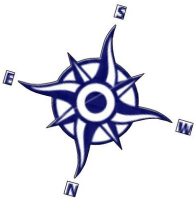

BUILDING FUNCTIONS

- 1 DIRECTOR, POLICE
- 2 EXTENDED CARE, NUCLEAR MED, DENTAL, K.T., P.T., O.T.
- 2A ADMISSIONS, EMER. RM., PATHOLOGY, RADIOLOGY IMAGING
- 4 MAIN KITCHEN, CANTEN, MEDICAL MEDIA
- 5 AUDITORIUM
- 7 LONG TERM EXTENDED PSYCHIATRIC, SOCIAL WORK
- 8 SUBSTANCE ABUSE, ACUTE PSYCHIATRIC
- 9 SUBSTANCE ABUSE, P.T.S.D.
- 10 CENTRALIZED FEE
- 11 MENTAL HYGIENE, DAY TREATMENT, PSYCHIATRY/PSYCHOLOGY ADMIN.
- 12 HOPTEL, PROSTHETICS, AFGE, EMP., HEALTH, C & P
- 13 BOILER/ CHILLED WATER PLANT
- 14 LAUNDRY
- 15 SOILED LINEN, VET. INDUST., ENG./MED. REC. STOR.
- 16 VISN 6 OFFICES, ADR, AC SHOP, LANDSCAPE

- 17 LEASED SPACE
- 18 OFFICES
- 19 OFFICES
- 23 SEWAGE PUMP HOUSE
- 24 STEEL WATER TANK & TOWER
- 25 DUPLEX HOUSE (LEASE)
- 26 6-CAR GARAGE
- 27 5-CAR GARAGE
- 28 5-CAR GARAGE

- 29 SWIMMING POOL
- 34 STORAGE
- 35 IMPLEMENT SHED
- 46 FLAGPOLE
- 72 STORAGE
- 74 FMS, LOGISTICS, SAFETY, HRM, IRS
- 75 WHEELCHAIR CLINIC, REGION OFFICE STO, FISCAL, FITNESS CNTR
- 76 RESEARCH, NATIONAL AFGE, CARPENTRY & ELECTRIC SHOPS, TRANSITIONAL LVG

- 77 CREDIT UNION, EDUCATION, ENVIRONMENTAL MGMT, STUDENT QUARTERS
- 80 GREENHOUSE (WEST)
- T85 SHEET METAL SHOP
- 121 GREENHOUSE
- 125 WATER TANK & TOWER
- 130 GRANDSTAND


- 131 ELECTRICAL SUBSTATION
- 133 GOLF CLUBHOUSE
- 138 EMERGENCY GENERATOR BLDG
- 139 EMERGENCY GENERATOR BLDG
- 140 EMERGENCY GENERATOR BLDG
- 141 EMERGENCY GENERATOR BLDG
- 142 EMERGENCY GENERATOR BLDG

- 143 MAIN HOSPITAL, OUTPATIENT, INPATIENT, CLINICAL NURSING UNIT.
- 144 CHAPEL
- 145 PLUMBING SHOP
- 146 CHAPEL OFFICES
- 148 MOTOR VEHICLE SHOP
- 150 SMOKING SHELTER
- 151 SMOKING SHELTER

- 153 EMERGENCY GENERATOR BLDG
- 154 EMERGENCY GENERATOR BLDG
- 155 PUMP HOUSE
- 156 EMERGENCY GENERATOR BLDG
- 157 EMERGENCY GENERATOR BLDG
- 158 SMOKING SHELTER
- 159 SMOKING SHELTER
- 160 OPEN FRONT SMOKING SHELTER
- 161 SMOKING SHELTER
- 162 ROANOKE CITY WATER MAIN BLDG
- 163 SALEM WATER MAIN BLDG
- 164 GREENHOUSE
- 165 OPEN SMOKING SHELTER
- 168 CENTER FOR TRAUMATIC STRESS
- 170 ACUTE INPATIENT PSYCHIATRIC UNIT
- 171 POLICE SUB STATION
- 172 WYVWA PUMP HOUSE
- 173 CITY OF SALEM PUMP HOUSE
- 174 WATER TOWER
- 175 NEW BOILER PLANT
- 176 SALT STORAGE BUILDING

UPDATED ON 05/09/2023
no scale

4/30/2026 3:30:20 PM
VA FORM 08-6231
Autosave Doc: \\24004_VA Salem Lobby\\24004_VA Salem Lobby.rvt

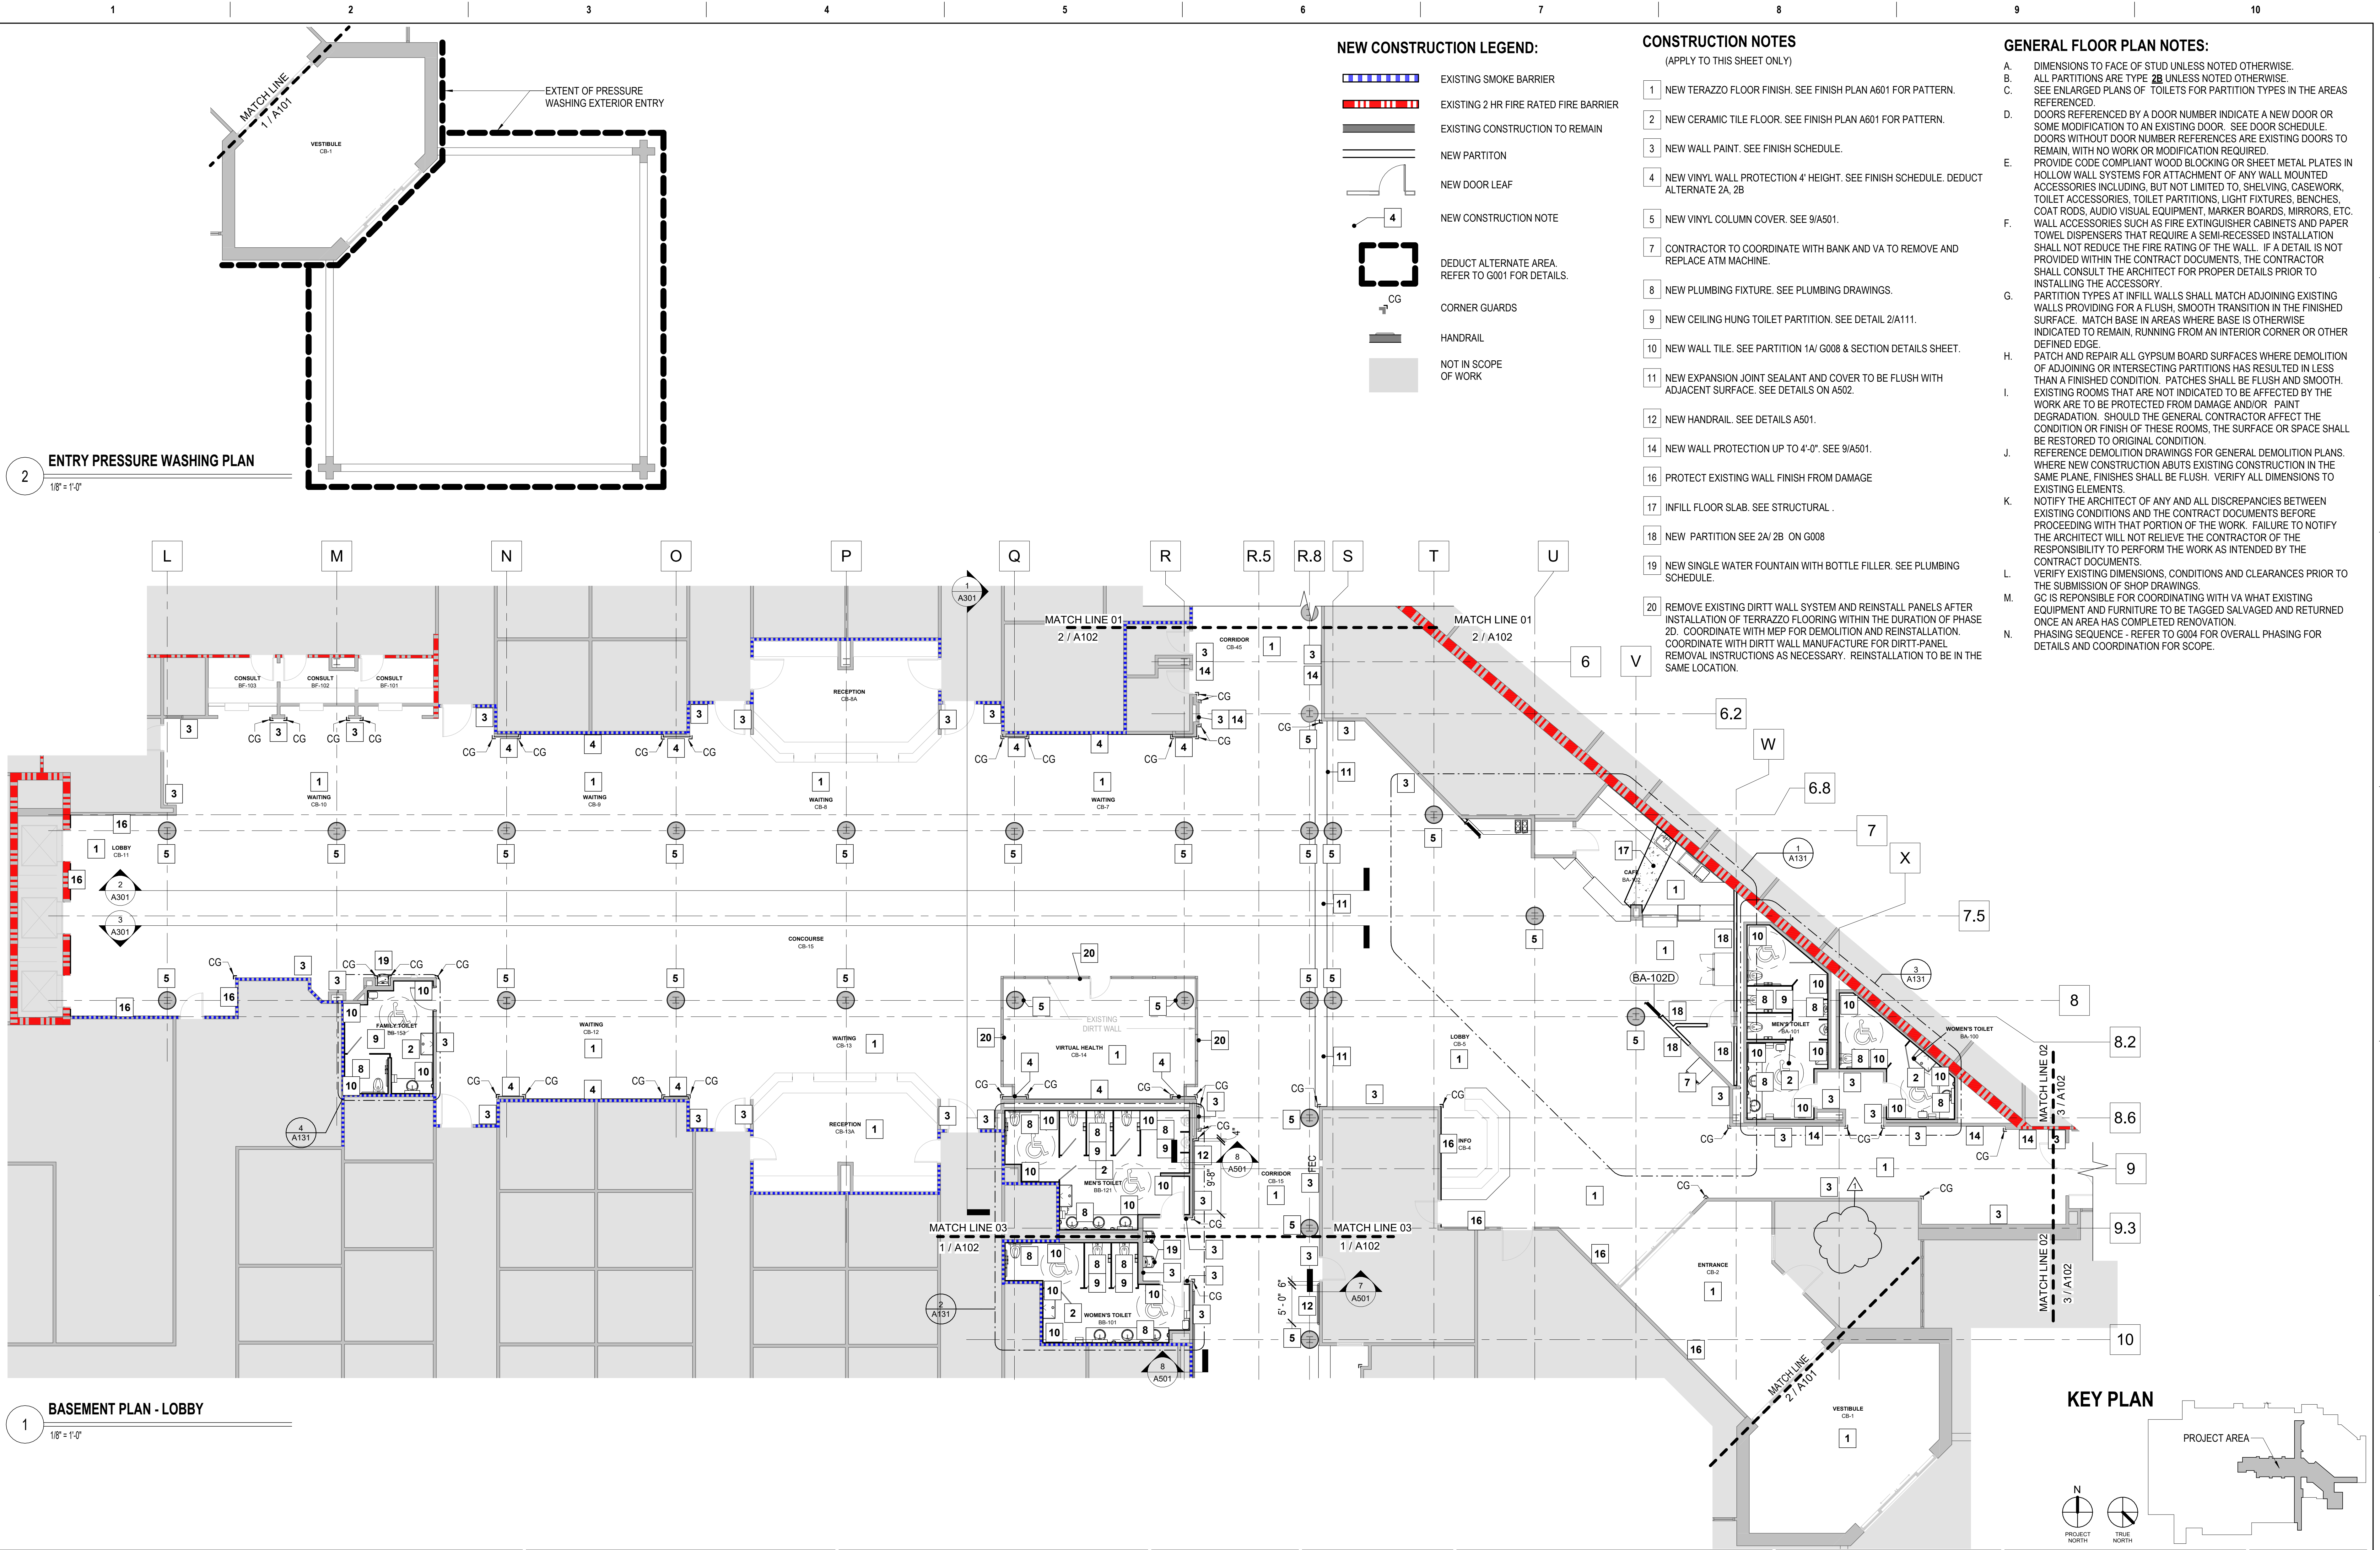

CONSULTANT		ARCHITECT/ENGINEER OF RECORD		Office of Construction and Facilities Management		Drawing Title BASEMENT PLAN - LOBBY		Phase 100% CONSTRUCTION DOCUMENTS		Project Title BUILDING 143 LOBBY RENOVATION 658-24-104		Drawing File Number 2621	
		THINKFORM DESIGN ARCHITECT LLC 38 EAST BROAD STREET HOPEWELL, NJ 08525 T:855.821.0274 F:609.644.4397 Russell DiNardo, AIA NY 031521-1		U.S. Department of Veterans Affairs		Approved:		Revision Number 1		Issue Date 09 JANUARY 2026		Drawing Number 143	
								Date 5/1/2026		Checked RD		Drawing JC	
								Revisions:				A101	
												SHEET 15 OF 59	



NOTE: SEE STRUCTURAL DETAILS


$$3'' = 1'-0''$$



1/8" = 1'-0"

(APPLY TO THIS SHEET ONLY)

- CAULKING RE APPLICATION TO BE SEALED WITH WEATHER-RESISTANT TO FULLL ANY GAPS FOR WATERTIGHT CONDITIONS.
- 28 LRP PANELS TO REMAIN. CONTRACTOR TO COORDINATE NEW ACT AND EXISTING LRP PANELS.

- A. IN ANY UNBRACED AREA OF CEILING WHICH IS LESS THAN 1000 SF, IT IS REQUIRED THAT SPRINKLER HEADS AND OTHER PENETRATIONS BE INSTALLED WITH A 2" OVERSIZED RING, SLEEVE, OR ADAPTER THROUGH THE CEILING TILE TO ALLOW FOR ONE INCH OF FREE MOVEMENT IN ALL HORIZONTAL DIRECTIONS.
- B. HEIGHT OF CEILING ABOVE FINISH FLOOR IS TAKEN FROM FLOOR SURFACE DIRECTLY BELOW.
- C. SUSPENSION GRIDS SHALL BE CENTERED IN ALL SPACES UNLESS INDICATED OTHERWISE ON ARCHITECTURAL RCP.
- D. ALL DEVICES MOUNTED IN ACOUSTICAL CEILING TILES SUCH AS LIGHTS, SPEAKERS, EXHAUST GRILLS, SPRINKLER HEADS, SMOKE DETECTORS, BELLS, TEST SWITCHES, OR FOR DUCT DETECTORS, ETC. SHALL BE CENTERED IN THE ACOUSTICAL CEILING TILE UNLESS OTHERWISE SPECIFIED SHALL BE INDEPENDENTLY SUPPORTED.
- E. SPRINKLER HEADS IN GYPSUM BOARD CEILINGS SHALL BE CENTERED AND ALIGN WITH RECESSED LIGHT FIXTURES IF APPLICABLE.
- F. PROVIDE CEILING ACCESS PANELS IN GWB CEILINGS TO PROVIDE ACCESS TO ELECTRICAL, MECHANICAL AND PLUMBING DEVICES THAT REQUIRE SERVICE FOR MAINTENANCE. CONFER WITH A/E PRIOR TO PLACEMENT.

	1 HOUR RATED FIRE BARRIER
	2 HOUR RATED FIRE BARRIER
	RATED SMOKE BARRIER
	NEW ACT 2' x 2' - ACOUSTIC CEILING TILE
	EXISTING ACT 2' x 2' - ACOUSTIC CEILING TILE
	EXISTING ACT 2' x 4' - ACOUSTIC CEILING TILE
	EXISTING GYP BOARD CEILING
	EXISTING 2 X 4 FIXTURE
	EXISTING 2 X 2 FIXTURE
	EXISTING RECESSED CAN FLUORESCENT LIGHT FIXTURE
	EXISTING SPRINKLER HEAD
	EXISTING MECHANICAL DIFFUSER
	EXISTING EXIT SIGN
	EXISTING RETURN GRILL
	EXISTING SUPPLY 2X2 DIFFUSER GRILL
	EXISTING SMOKE DETECTOR
	EXISTING SPEAKER
	EXISTING EXPANSION JOINT COVER
	EXISTING 1' X 4' LIGHT FIXTURE
	EXISTING 6" RECESSED CAN LIGHT
	EXISTING 12" EXHAUST GRILLE. SEE MECHANICAL DRAWINGS
	EXISTING 2 X 4 FIXTURE
	NEW 2 X 2 FIXTURE
	NEW RECESSED CAN FLUORESCENT LIGHT FIXTURE
	NEW MECHANICAL DIFFUSER
	NEW 12" PENDANT LIGHT
	NEW SUPPLY 2X2 DIFFUSER GRILL

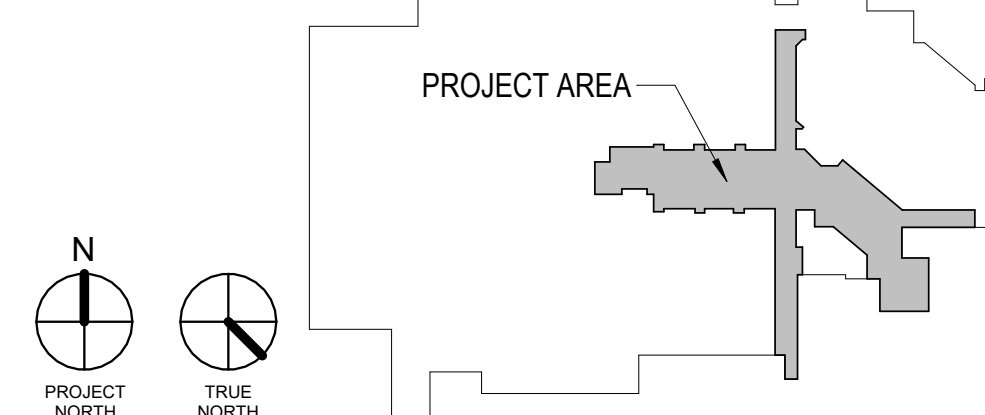

BASEMENT RCP - LOBBY

1/8" = 1'-0"

A111

SHEET 17 OF 59

4/30/2026 3:30:25 PM
VA FORM 08-6231
Autosave Doc: 24004 VA Salem Lobby/24004 VA Salem Lobby.rvt

1 2 3 4 5 6 7 8 9 10

A
B
C
D
E
F

A
B
C
D
E
F

CONSTRUCTION NOTES

(APPLY TO THIS SHEET ONLY)

- 8 NEW ACOUSTICAL CEILING.
- 9 NEW CEILING HUNG TOILET PARTITION. SEE DETAIL 2/A111.
- 11 NEW EXPANSION JOINT SEALANT AND COVER.
- 16 NEW MECHANICAL GRILLS. SEE MECHANICAL DRAWINGS
- 17 EXISTING LIGHT TO BE MOVED TO CENTER OF CORRIDOR.
- 28 LRP PANELS TO REMAIN. CONTRACTOR TO COORDINATE NEW ACT AND EXISTING LRP PANELS.



GENERAL RCP NOTES:

- A. IN ANY UNBRACED AREA OF CEILING WHICH IS LESS THAN 1000 SF, IT IS REQUIRED THAT SPRINKLER HEADS AND OTHER PENETRATIONS BE INSTALLED WITH A 2" OVERSIZED RING, SLEEVE, OR ADAPTER THROUGH THE CEILING TILE TO ALLOW FOR ONE INCH OF FREE MOVEMENT IN ALL HORIZONTAL DIRECTIONS.
- B. HEIGHT OF CEILING ABOVE FINISH FLOOR IS TAKEN FROM FLOOR SURFACE DIRECTLY BELOW.
- C. SUSPENSION GRIDS SHALL BE CENTERED IN ALL SPACES UNLESS INDICATED OTHERWISE ON ARCHITECTURAL RCP.
- D. ALL DEVICES MOUNTED IN ACOUSTICAL CEILING TILES SUCH AS LIGHTS, SPEAKERS, EXHAUST GRILLES, SPRINKLER HEADS, SMOKE DETECTORS, REMOTE TEST SWITCHES FOR DUCT DETECTORS, ETC. SHALL BE CENTERED IN THE ACOUSTICAL CEILING TILE U.N.O. ALL DEVICES SHALL BE INDEPENDENTLY SUPPORTED.
- E. SPRINKLER HEADS IN GYPSUM BOARD CEILINGS SHALL BE CENTERED AND ALIGN WITH RECESSED LIGHT FIXTURES IF APPLICABLE.
- F. PROVIDE CEILING ACCESS PANELS IN GWB CEILINGS TO PROVIDE ACCESS TO ELECTRICAL, MECHANICAL AND PLUMBING DEVICES THAT REQUIRE SERVICE FOR MAINTENANCE. CONFER WITH A/E PRIOR TO PLACEMENT.


RCP LEGEND:

- 1 HOUR RATED FIRE BARRIER
- 2 HOUR RATED FIRE BARRIER
- RATED SMOKE BARRIER
- NEW ACT 2' x 2' - ACOUSTIC CEILING TILE
- EXISTING ACT 2' x 2' - ACOUSTIC CEILING TILE
- EXISTING ACT 2' x 4' - ACOUSTIC CEILING TILE
- EXISTING GYP BOARD CEILING
- EXISTING 2 X 4 FIXTURE
- EXISTING 2 X 2 FIXTURE
- EXISTING RECESSED CAN FLUORESCENT LIGHT FIXTURE
- EXISTING SPRINKLER HEAD
- EXISTING MECHANICAL DIFFUSER
- EXISTING EXIT SIGN
- EXISTING RETURN GRILL
- EXISTING SUPPLY 2X2 DIFFUSER GRILL
- EXISTING SMOKE DETECTOR
- EXISTING SPEAKER
- EXISTING EXPANSION JOINT COVER
- EXISTING 1' X 4' LIGHT FIXTURE
- EXISTING 6" RECESSED CAN LIGHT
- EXISTING 12" EXHAUST GRILLE, SEE MECHANICAL DRAWINGS
- EXISTING 2 X 4 FIXTURE
- NEW 2 X 2 FIXTURE
- NEW RECESSED CAN FLUORESCENT LIGHT FIXTURE
- NEW MECHANICAL DIFFUSER
- NEW 12" PENDANT LIGHT
- NEW SUPPLY 2X2 DIFFUSER GRILL


KEY PLAN

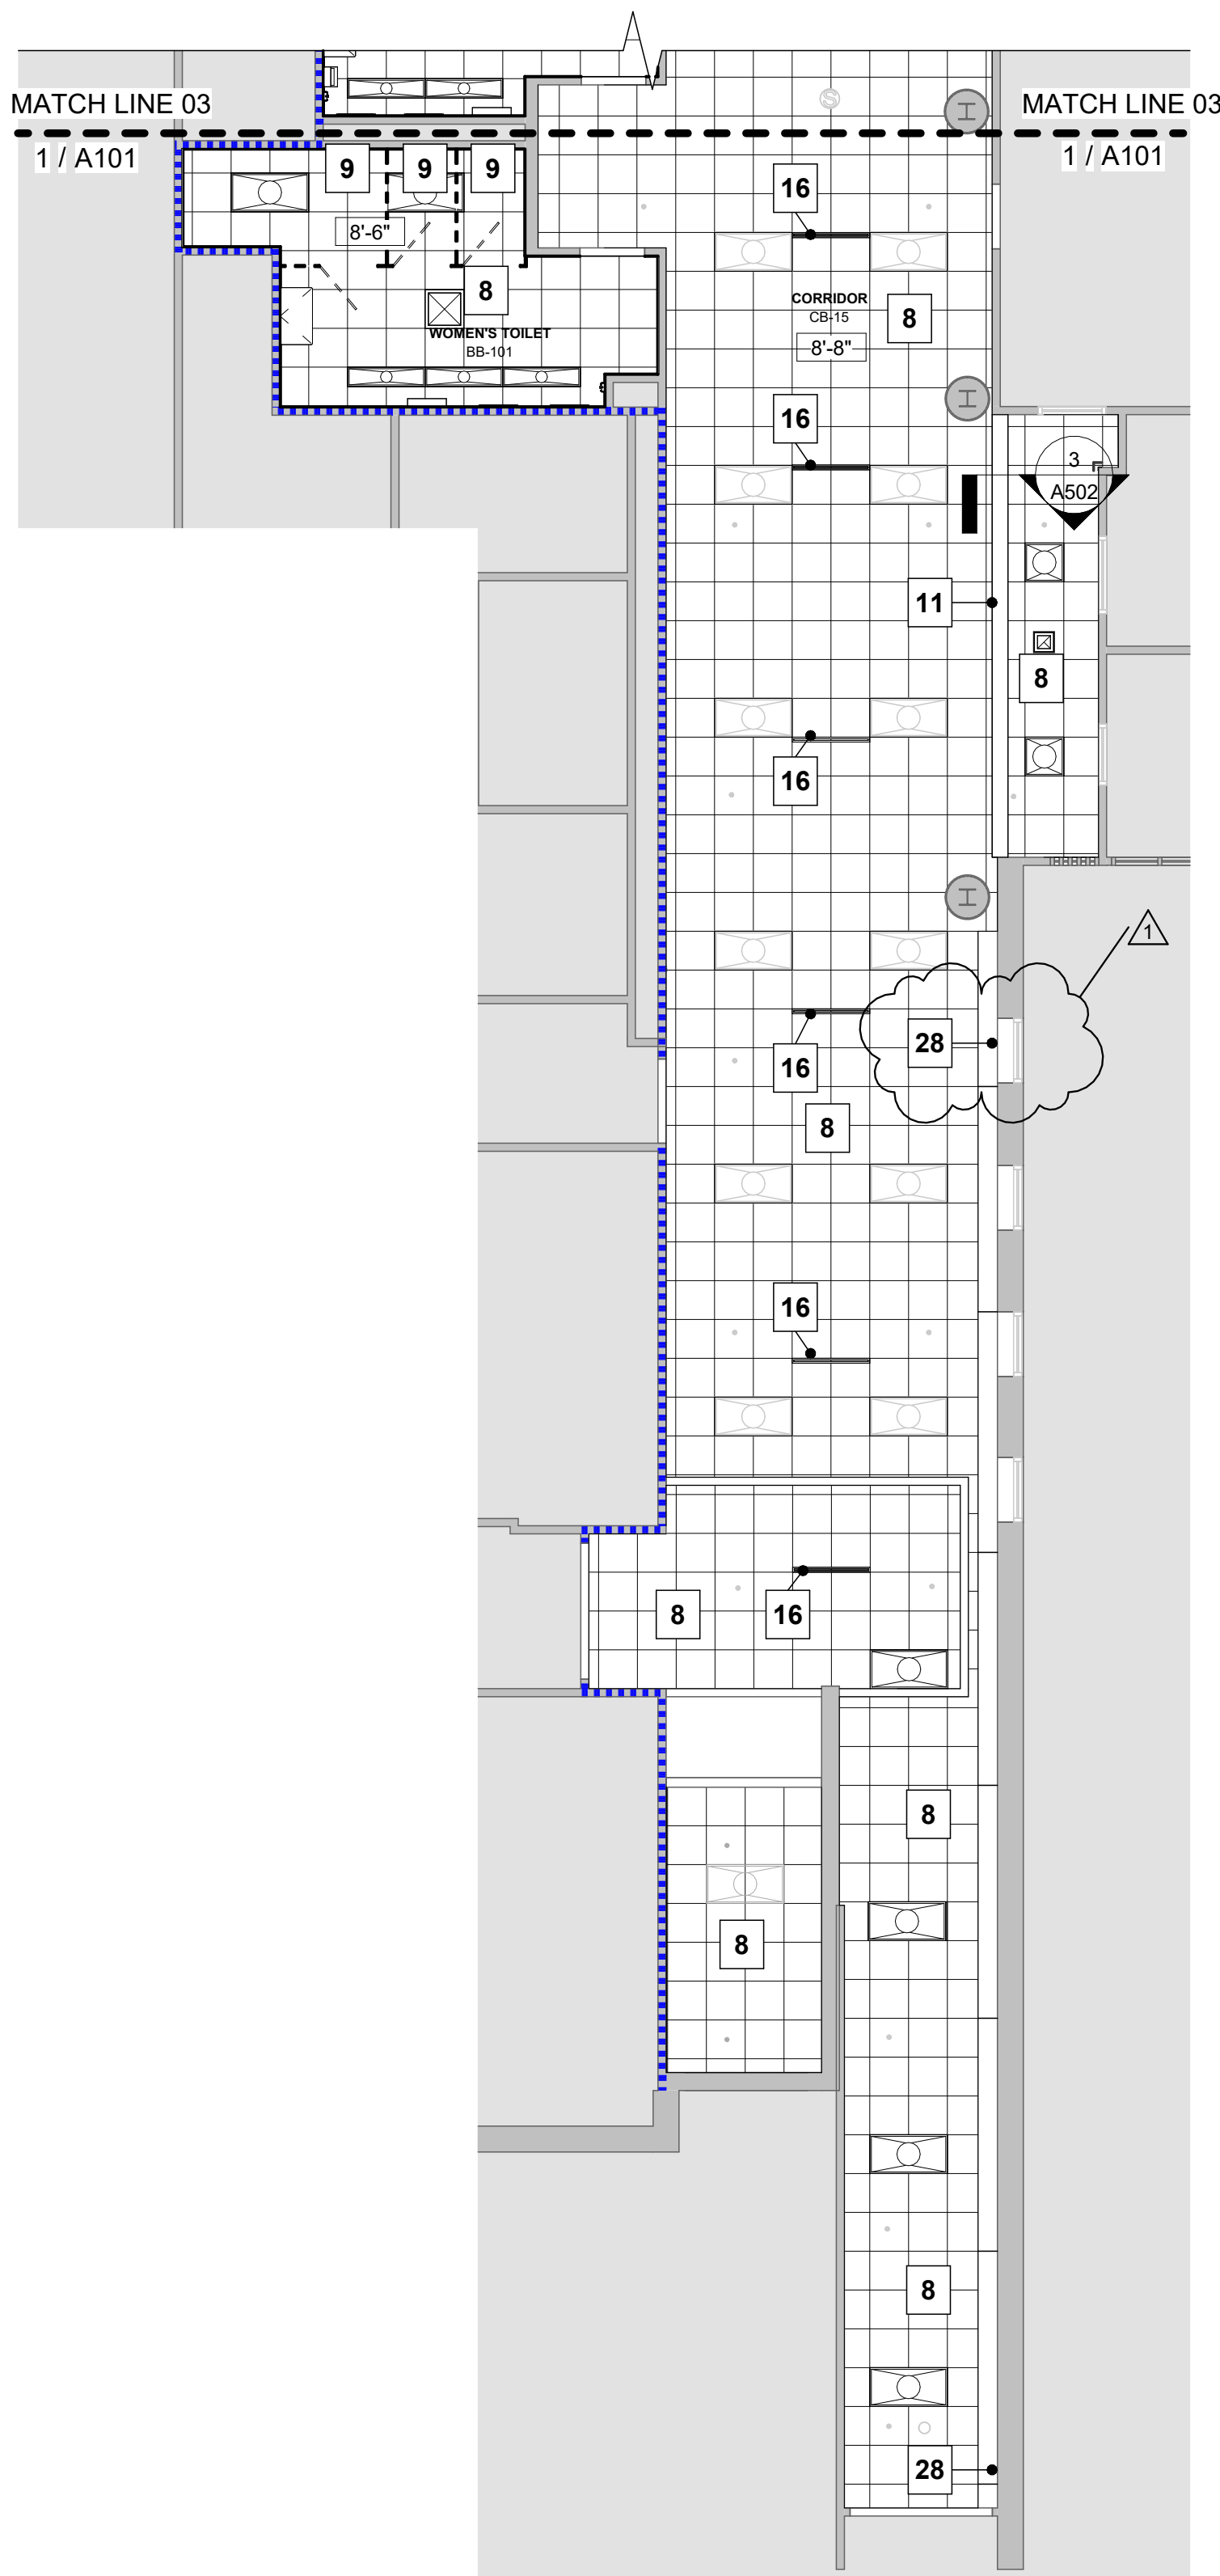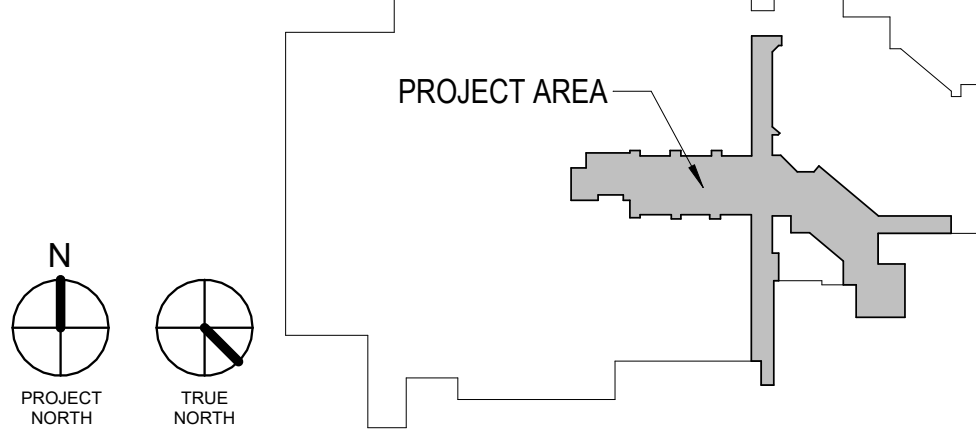

1 BASEMENT RCP CORRIDOR CB-15
1/8" = 1'-0"

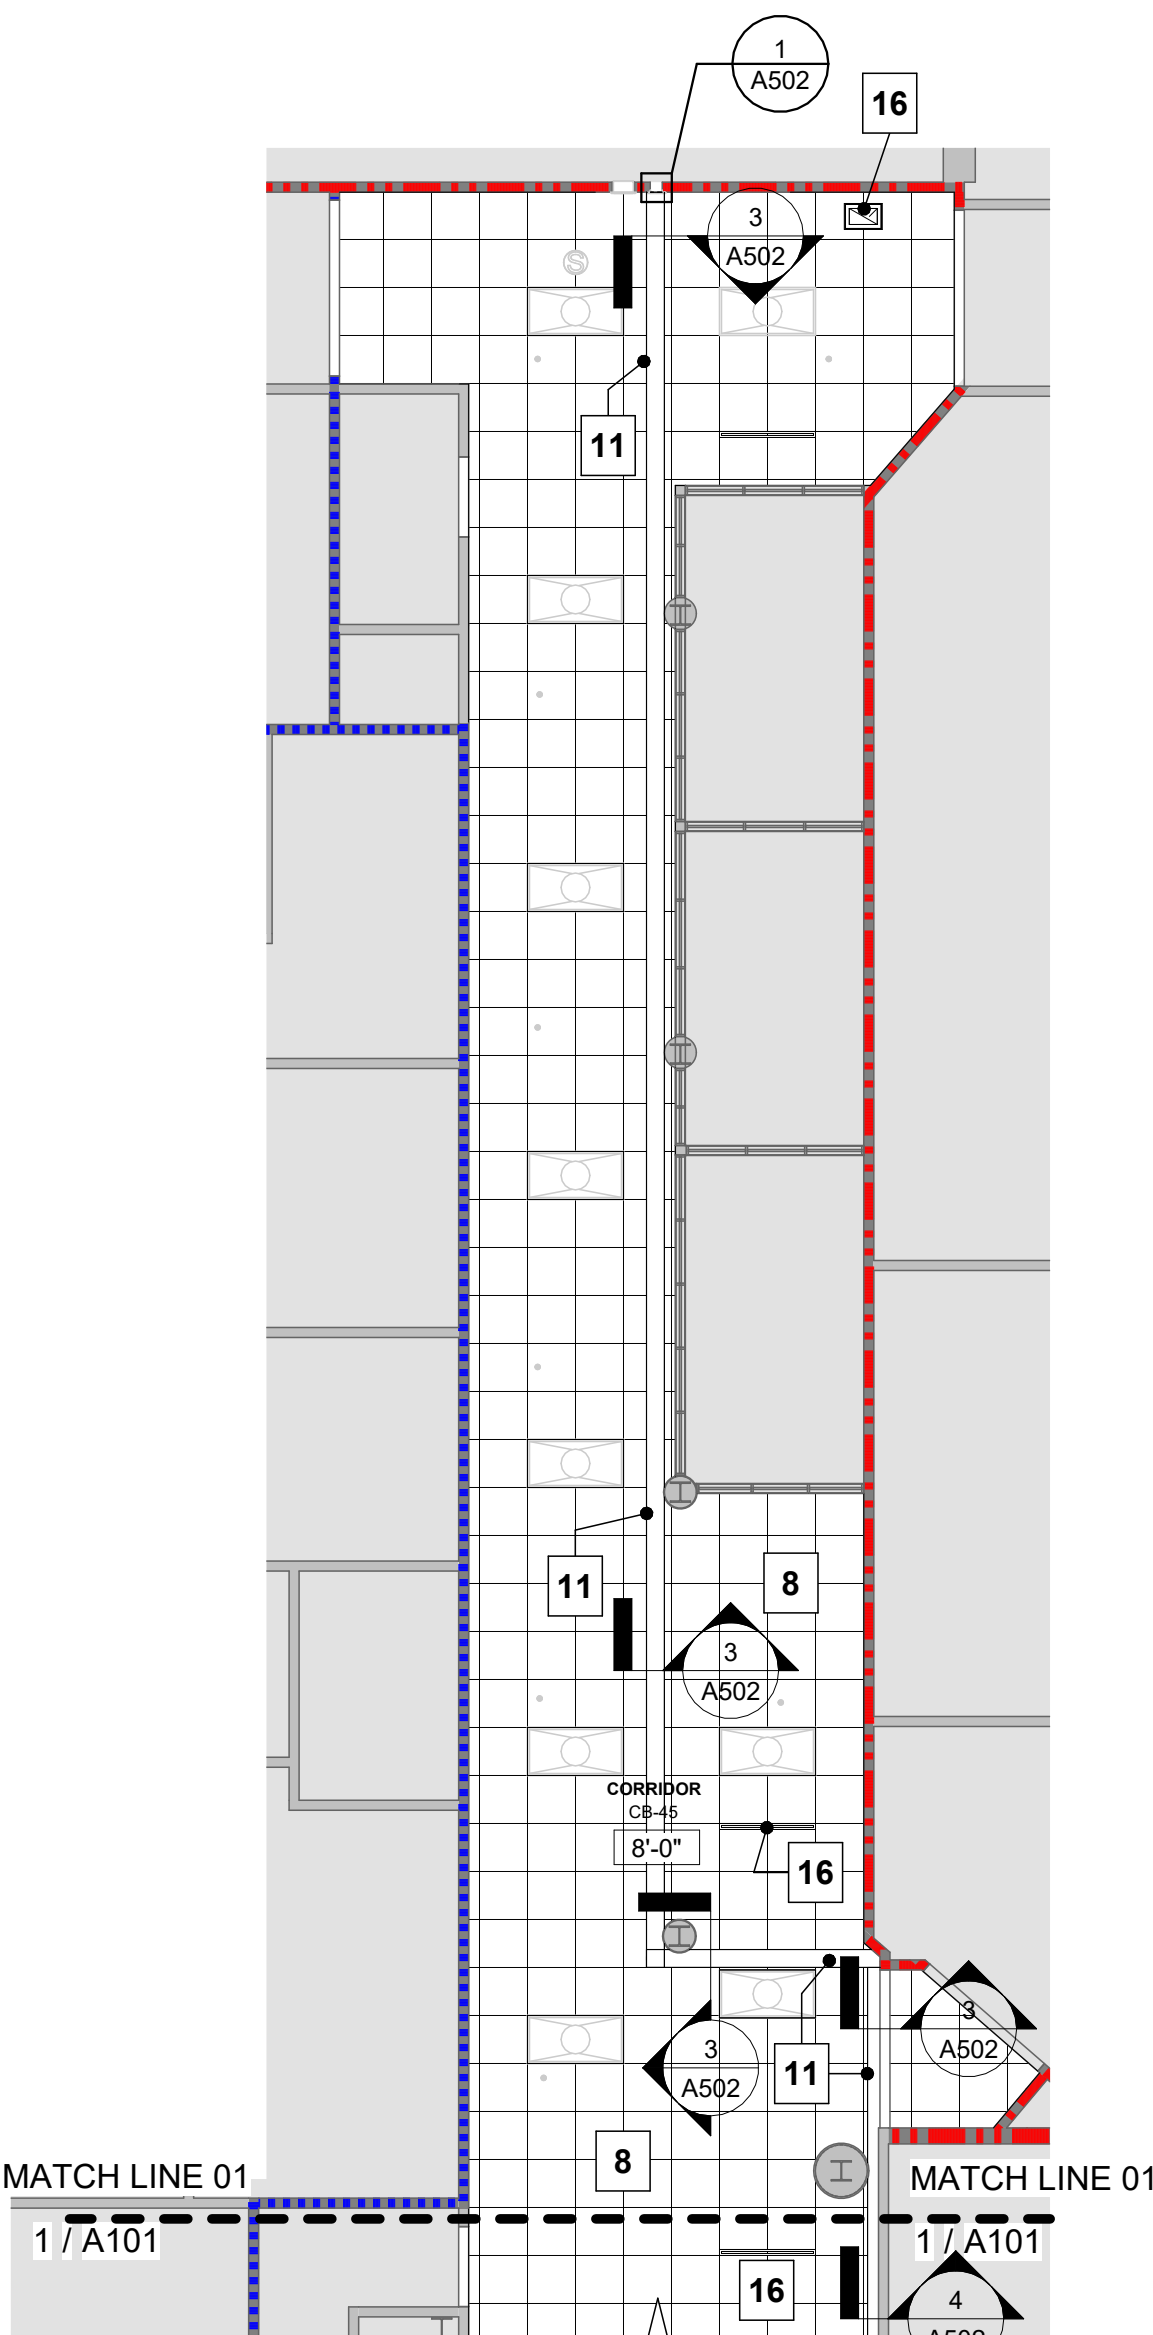

2 BASEMENT RCP CORRIDOR CB-45
1/8" = 1'-0"

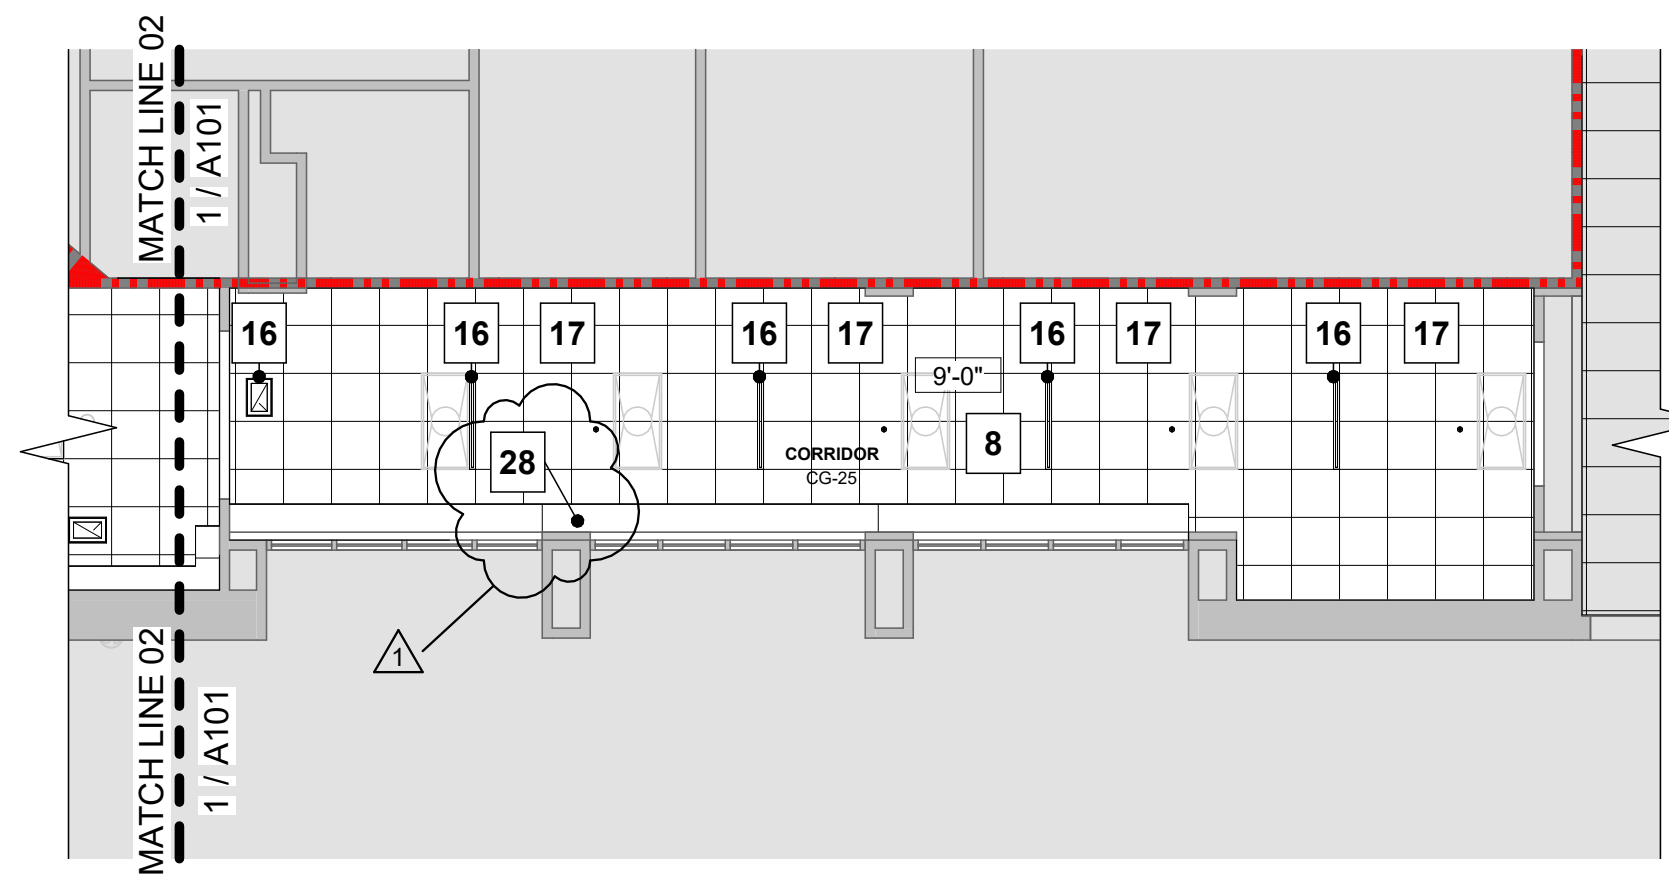

3 BASEMENT RCP CORRIDOR CG-25
1/8" = 1'-0"

CONSULTANT

ARCHITECT/ENGINEER OF RECORD

STAMP

Office of
Construction
and Facilities
Management



U.S. Department
of Veterans Affairs

Drawing Title

BASEMENT RCP - CORRIDORS

Approved:

Phase

100% CONSTRUCTION
DOCUMENTS

1

Revision

Number

5/1/2026

Date:

PreBid

Revisions:

Project Title

BUILDING 143 LOBBY
RENOVATION
658-24-104

Location

SALEM VA MEDICAL CENTER
1970 ROANOKE BLVD, SALEM, VA 24153-6406

Issue Date

09 JANUARY 2026

Checked

RD

Drawn

JC

Drawing File Number

2621

Building Number

143

Drawing Number

A112

SHEET 18 OF 59