



UNITED STATES DEPARTMENT OF STATE

OBO Regional Support Center (ORSC)
U.S. Consulate General Frankfurt

CHIEF OF MISSION RESIDENCE BATHROOM RENOVATION

U.S. EMBASSY
LJUBLJANA, SLOVENIA

DRAWING INDEX:

- G00

A00

A01

A02

A03

A04

A05

A06
- COVER PAGE

PROJECT AREA

BATHROOOM FLOORPLAN

ELEVATIONS - EXISTING

ELEVATIONS 1 & 2 - NEW BATHROOM

ELEVATIONS 3 & 4 - NEW BATHROOM

REFLECTIVE CEILING PLAN & SHOWER DETAILS

PRODUCTS LIST



UNITED STATES DEPARTMENT OF STATE
OBO Regional Support Center (ORSC)
U.S. Consulate General Frankfurt

CHIEF OF MISSION RESIDENCE
BATHROOM RENOVATION

for
U.S. EMBASSY
LJUBLJANA, SLOVENIA

WARNING : This Document is the property of the U.S. Government. Further reproduction and / or distribution outside the contract team is prohibited without express written approval of: Office of Foreign Buildings Operations, U.S. Department of State, Washington, DC, 20522-0620. Information on this document is not to be altered except with the written approval of the individual whose seal appears hereon.

Rev Number	Description	Date
REVISIONS		

KEY PLAN

RELEASE FOR CONSTRUCTION


DRAWING TITLE

COVER

FBO PROJECT NUMBER	DRAWING SCALE	PHASE
	1:1	
CADD FILE NAME	CADD PLOT SCALE	☐ CONCEPT ☐ 35% ☐ 60% ☐ 90% ☐ 100% ☒ FINAL
LIJ_CMR_SECOND_FLOOR_BATHROOM	1:25	

	DATE	G00
	April 28, 2026	
	DRAWN BY	
	Ntouneta, M	
	CHECKED BY	
	PROJECT NUMBER	
	CLASSIFICATION	
	SENSITIVE BUT UNCLASSIFIED	

PLAN A00 SECOND FLOOR PLAN
SCALE 1 : 100

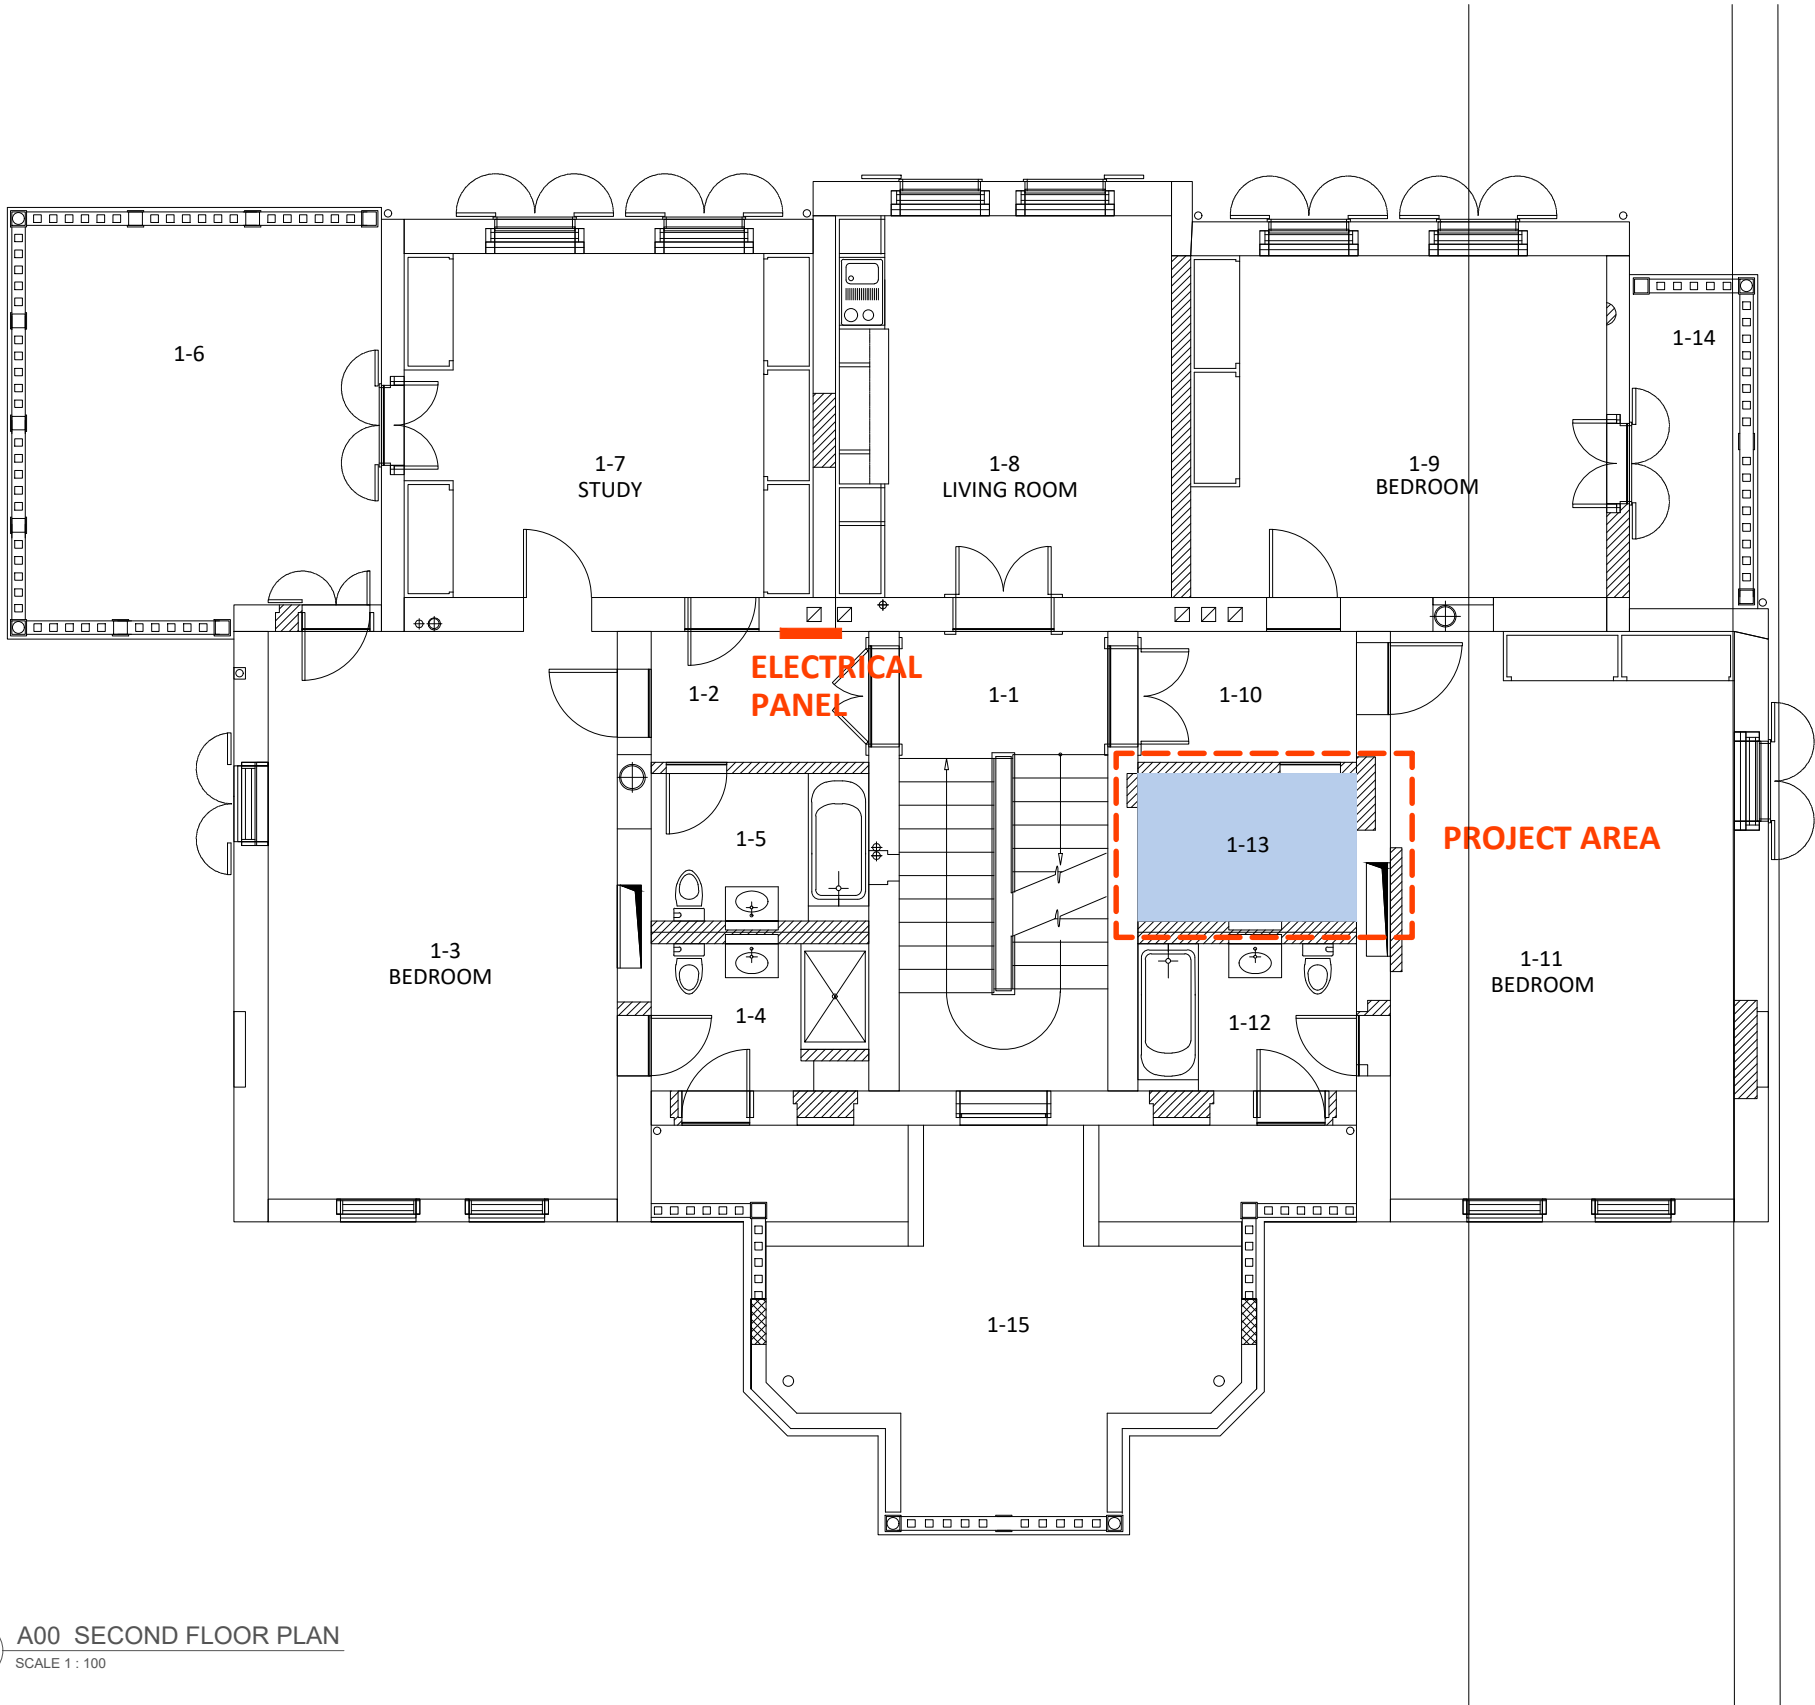

UNITED STATES DEPARTMENT OF STATE
OBO Regional Support Center (ORSC)
U.S. Consulate General Frankfurt

CHIEF OF MISSION RESIDENCE
BATHROOM RENOVATION

for
U.S. EMBASSY
LJUBLJANA, SLOVENIA

WARNING : This Document is the property of the U.S. Government. Further reproduction and / or distribution outside the contract team is prohibited without express written approval of: Office of Foreign Buildings Operations, U.S. Department of State, Washington, DC, 20522-0620. Information on this document is not to be altered except with the written approval of the individual whose seal appears hereon.

Rev Number	Description	Date
------------	-------------	------

REVISIONS

KEY PLAN

RELEASE FOR CONSTRUCTION

DRAWING TITLE

SECOND FLOOR PLAN
PROJECT AREA

FBO PROJECT NUMBER	DRAWING SCALE	PHASE
--------------------	---------------	-------

CADD FILE NAME	CADD PLOT SCALE	☐ CONCEPT ☐ 35% ☐ 60% ☐ 90% ☐ 100% ☒ FINAL
----------------	-----------------	---

LJU_CMR_SECOND_FLOOR_BATHROOM

DATE

April 28, 2026

DRAWN BY

Ntouneta, M

CHECKED BY

PROJECT NUMBER


CLASSIFICATION

SENSITIVE BUT UNCLASSIFIED


A00

1. Verify all existing conditions prior to performing any work.
2. Coordinate all power outage with the government in advance.
3. Coordinate all demolition work prior to beginning work to avoid shutting down adjacent areas.
4. For devices shown as being demolished, remove electrical devices, wiring, and raceway in walls and ceilings back to source or nearest device. Do not abandon any conductors. Where conduits are concealed in walls/floor, remove wiring and cut conduit flushed with walls or floor.


1. Remove existing receptacle, box, conduit, and wires to the nearest device. Modify branch feeder as required

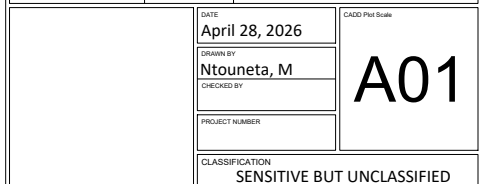


A01

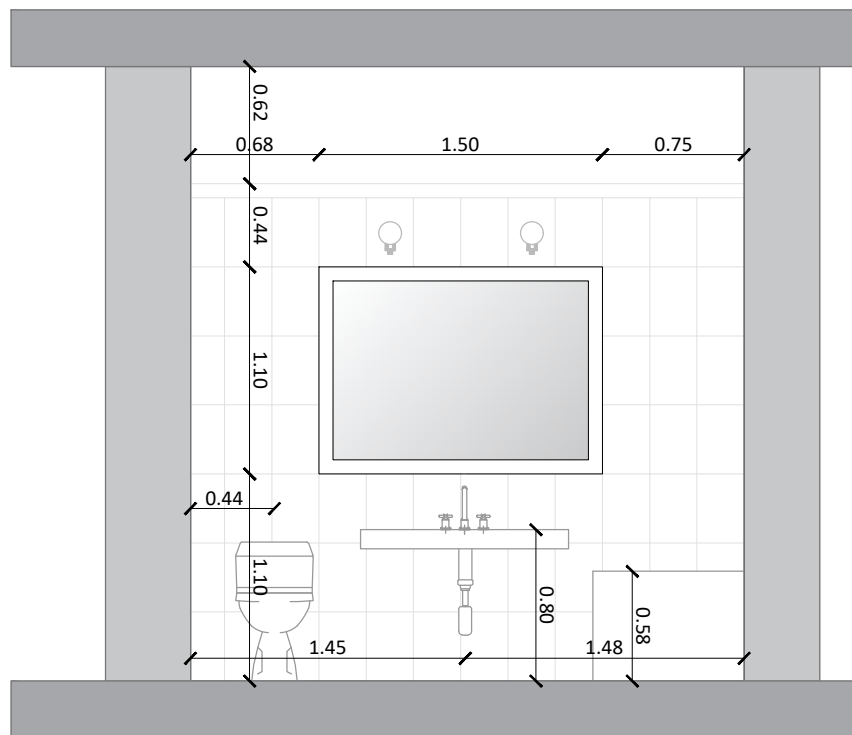


EL 1 EXISTING
SCALE 1 : 40

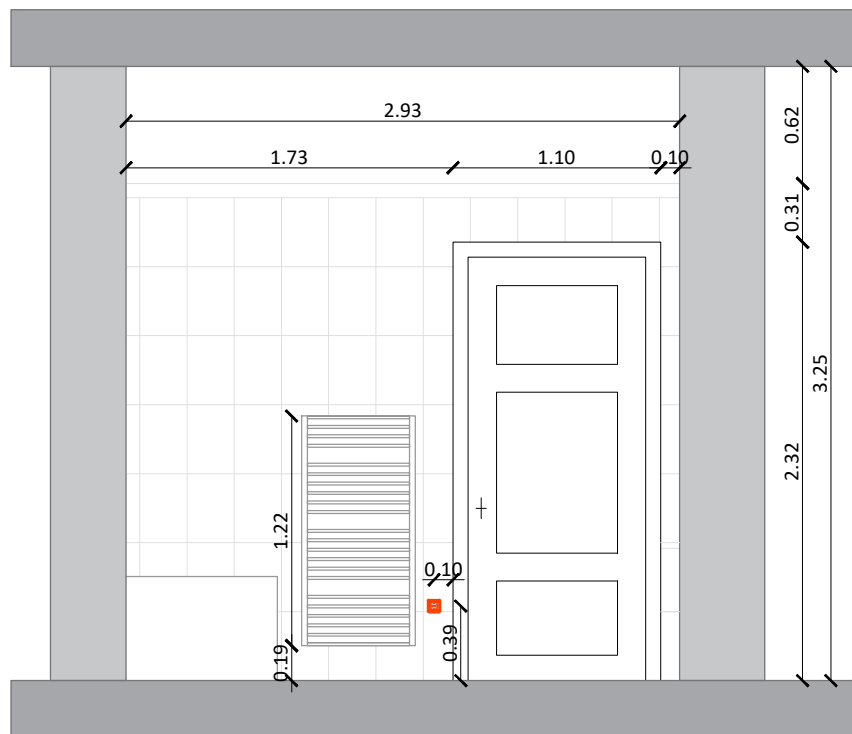

EL 3 EXISTING
SCALE 1 : 40

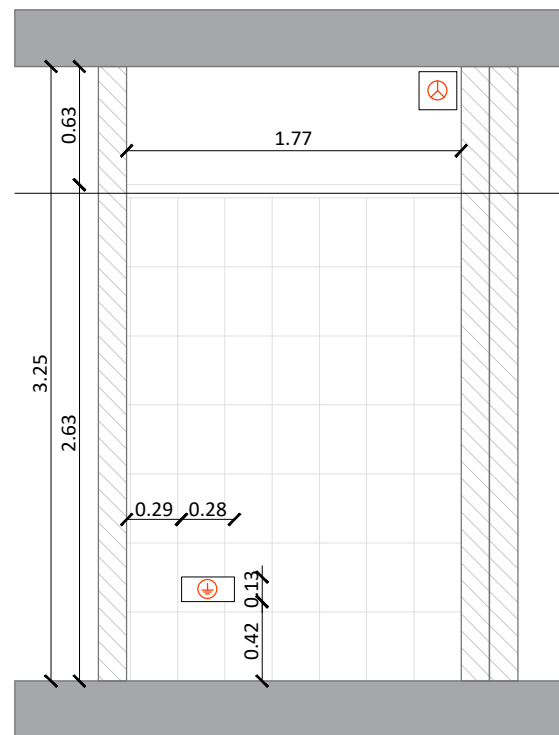

EL 2 EXISTING
SCALE 1 : 40

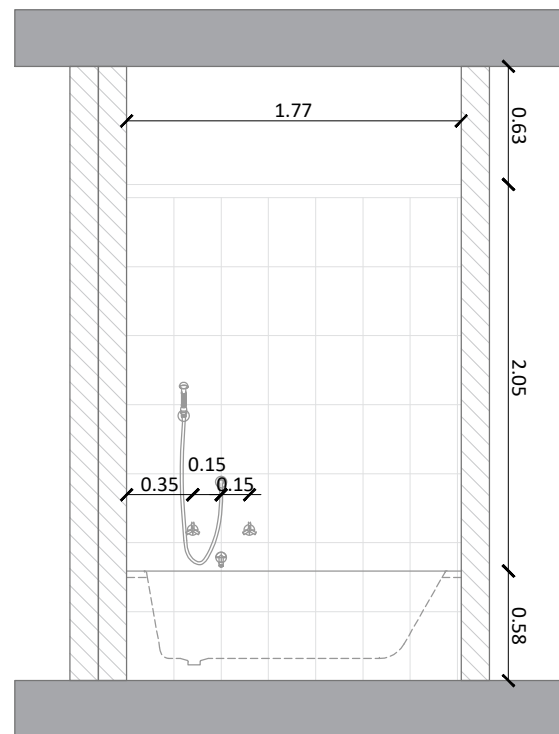

EL 4 EXISTING
SCALE 1 : 40



UNITED STATES DEPARTMENT OF STATE
OBO Regional Support Center (ORSC)
U.S. Consulate General Frankfurt

CHIEF OF MISSION RESIDENCE
BATHROOM RENOVATION

for
U.S. EMBASSY
LJUBLJANA, SLOVENIA

WARNING : This Document is the property of the U.S. Government. Further reproduction and / or distribution outside the contract team is prohibited without express written approval of: Office of Foreign Buildings Operations, U.S. Department of State, Washington, DC, 20522-0620. Information on this document is not to be altered except with the written approval of the individual whose seal appears hereon.



SINGLE RECEPTACLE



GROUND WIRE



EXHAUST FAN

Rev Number	Description	Date

KEY PLAN


RELEASE FOR CONSTRUCTION

DRAWING TITLE


BATHROOM 1-13
ELEVATIONS - EXISTING

FBO PROJECT NUMBER	DRAWING SCALE 1:1	PHASE
CADD FILE NAME UU_CMR_SECOND FLOOR_BATHROOM	CADD PLOT SCALE 1:40	☐ CONCEPT ☐ 35% ☐ 60% ☐ 90% ☐ 100% ☒ FINAL

	DATE	April 28, 2026	CADD Plot Scale A02
	DRAWN BY	Ntouneta, M	
	CHECKED BY		
	PROJECT NUMBER		
CLASSIFICATION		SENSITIVE BUT UNCLASSIFIED	

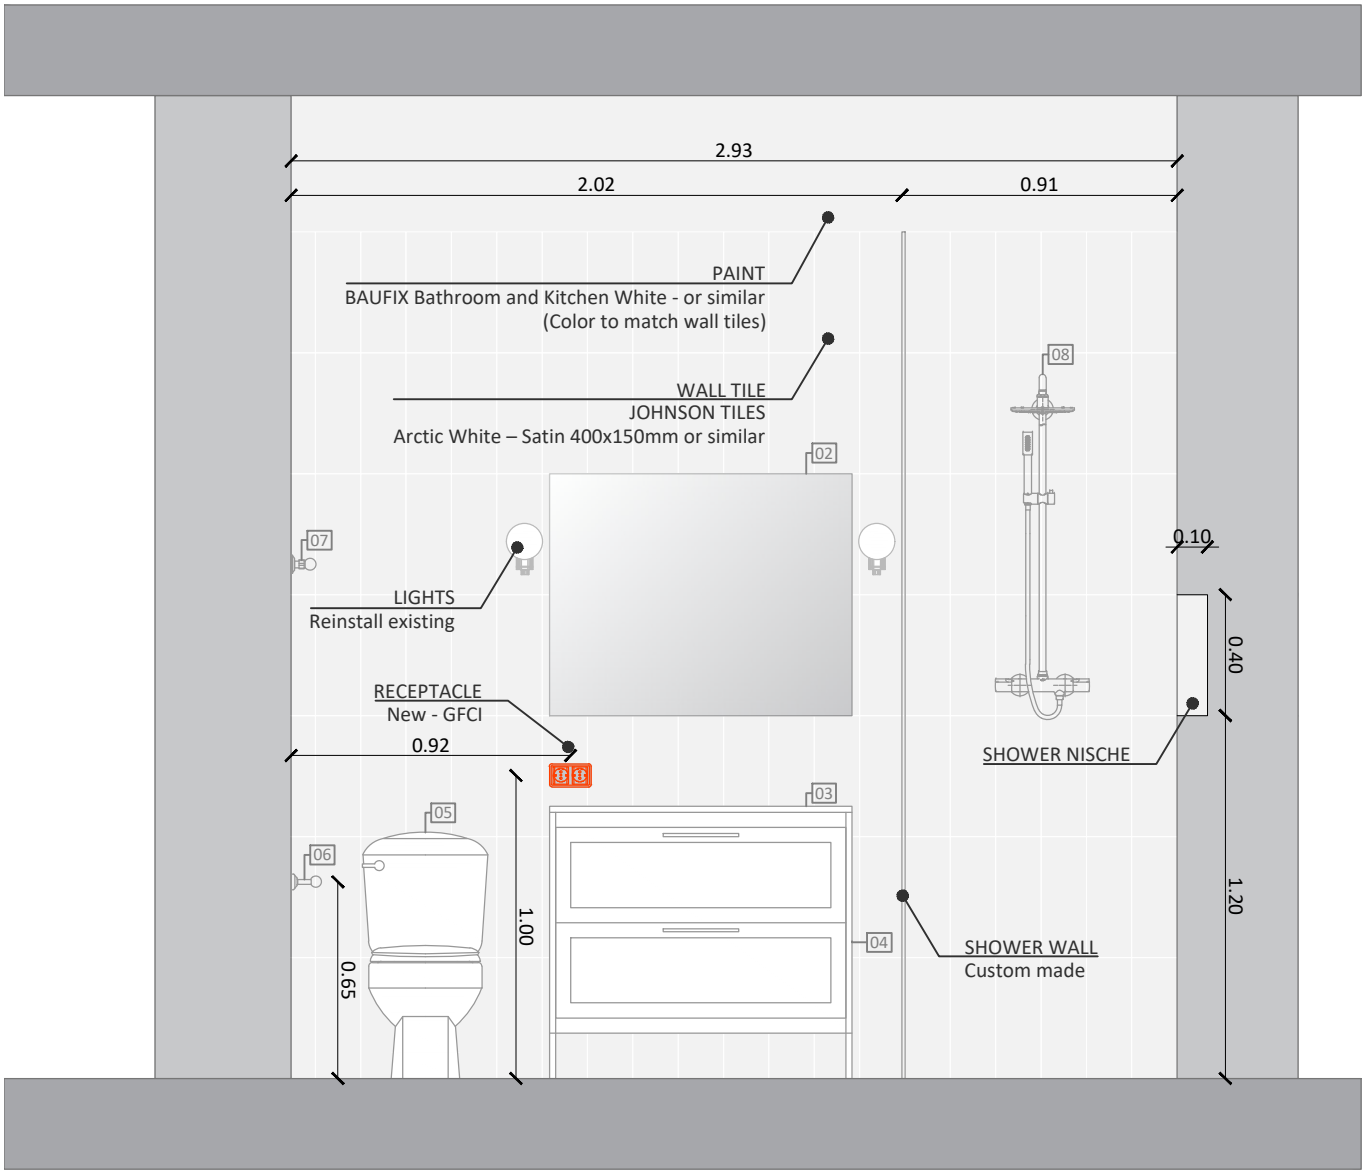

EL 1 NEW BATHROOM
SCALE 1 : 25

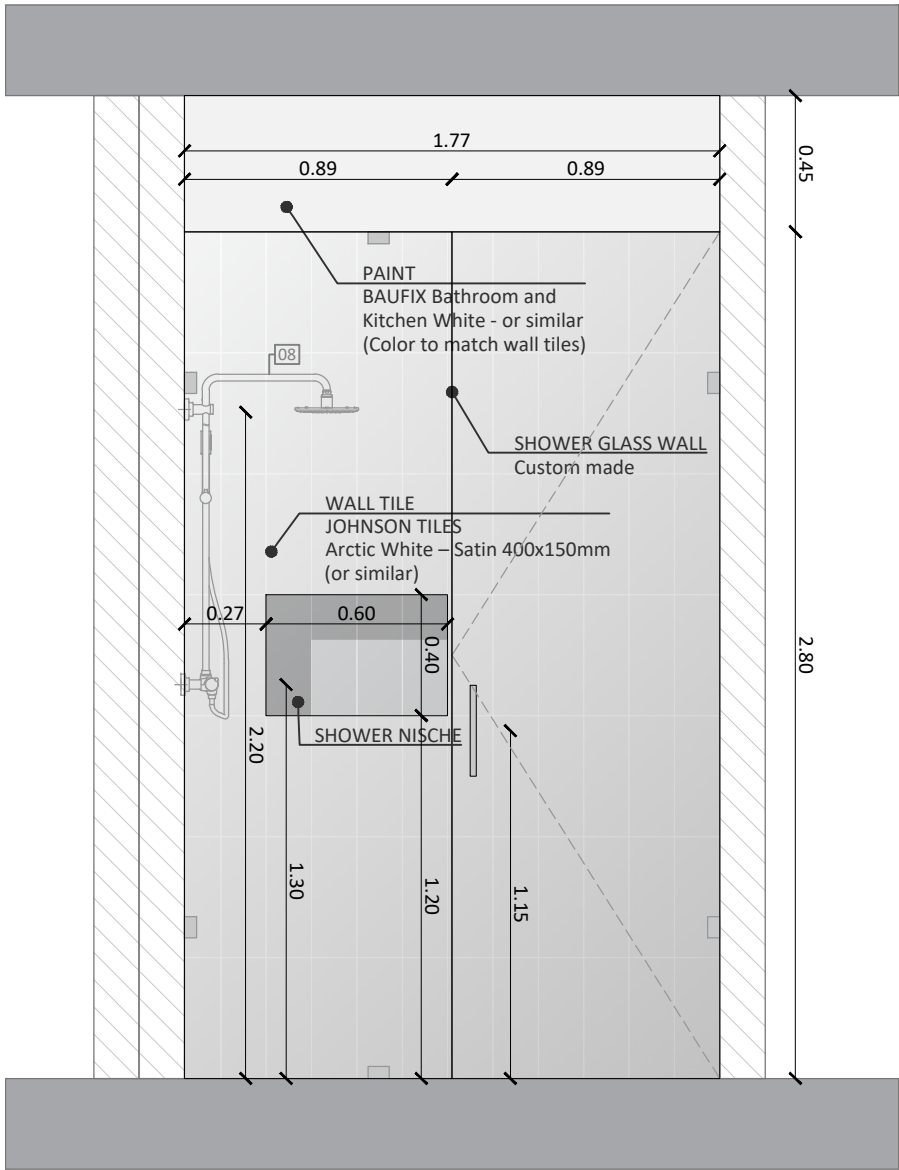

EL 2 NEW BATHROOM
SCALE 1 : 25



UNITED STATES DEPARTMENT OF STATE
OBO Regional Support Center (ORSC)
U.S. Consulate General Frankfurt

CHIEF OF MISSION RESIDENCE
BATHROOM RENOVATION

for
U.S. EMBASSY
LJUBLJANA, SLOVENIA

WARNING : This Document is the property of the U.S. Government. Further reproduction and / or distribution outside the contract team is prohibited without express written approval of: Office of Foreign Buildings Operations, U.S. Department of State, Washington, DC, 20522-0620. Information on this document is not to be altered except with the written approval of the individual whose seal appears hereon.



DOUBLE RECEPTACLE
GFCI

Rev Number	Description	Date

REVISIONS

KEY PLAN

RELEASE FOR CONSTRUCTION

DRAWING TITLE

BATHROOM 1-13
ELEVATIONS 1 & 2

FBO PROJECT NUMBER	DRAWING SCALE	PHASE
	1:1	

CADD FILE NAME	CADD PLOT SCALE	☐ CONCEPT ☐ 25% ☐ 50% ☐ 75% ☐ 100% ☒ FINAL
LJU_CMR_SECOND_FLOOR_BATHROOM	1:25	


DATE	CADD Plot Scale
April 28, 2026	

DRAWN BY	CHECKED BY
Ntouneta, M	

PROJECT NUMBER

CLASSIFICATION
SENSITIVE BUT UNCLASSIFIED

A03

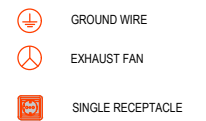

Rev Number	Description	Date
REVISIONS		

KEY PLAN

RELEASE FOR CONSTRUCTION

DRAWING TITLE	
---------------	--

FBO PROJECT NUMBER	DRAWING SCALE 1:1	PHASE
CADD FILE NAME LUU_OMR_SECOND FLOOR_BATHROOM	CADD PLOT SCALE 1:25	☐ CONCEPT ☐ 35% ☐ 60% ☐ 90% ☐ 100% ☒ FINAL

	DATE	April 28, 2026	CADD Plot Scale	A04
	DRAWN BY	Ntouneta, M		
	CHECKED BY			
	PROJECT NUMBER			
	CLASSIFICATION	SENSITIVE BUT UNCLASSIFIED		

	1	2	3	4	5	6	7	8	9	10	11	12	13	14
L														
K														
J														
I														
H														
G														
F														
E														
D														
C														
B														
A														
	1	2	3	4	5	6	7	8	9	10	11	12	13	14

PRODUCTS LIST						
	PRODUCT NAME		PRODUCT NAME	MODEL	DIMENTIONS	COLOR
1	GEBERIT		CleanLine20	A06340	90 x 4.7 cm	Brushed Steel
2	COYCAMA		SUN	20400100	100 x 80 cm	Mirror
3	COYCAMA		ONIX NEW	55001101	100(70+30) x 46.5 cm	White
4	COYCAMA		TOSCANA.100	19737100	100 x 45 x 89 cm	White matt with black faucet, legs and handles
5	CONCEPT+		ARROW	V455588	65 x 78 x 37 cm	White
6	VOXORT		INGRID	V459940	16 x 10 x 8.8 cm	Chrome
7	VOXORT		3600	N13106	60 x 6.5 cm	Chrome
8	GROHE		PROPITERM	V451439	113 x 4.12 x 30.4 cm	Chrome
9	TERMbad			G62290	120 x 60 cm	White
	TILES LIST					
10	FLOOR	MARCA CORONA	STONECLOUD	NATURALE MATT	120 x 60cm	Blue
11	WALLS	JOHNSON TILES	ARCTIC WHITE	TNS01A	40 x 15cm	White

 UNITED STATES DEPARTMENT OF STATE OBO Regional Support Center (ORSC) U.S. Consulate General Frankfurt		
CHIEF OF MISSION RESIDENCE BATHROOM RENOVATION for U.S. EMBASSY LJUBLJANA, SLOVENIA		
WARNING : This Document is the property of the U.S. Government. Further reproduction and / or distribution outside the contract team is prohibited without express written approval of: Office of Foreign Buildings Operations, U.S. Department of State, Washington, DC, 20522-0620. Information on this document is not to be altered except with the written approval of the individual whose seal appears hereon.		
Rev Number	Description	Date
REVISIONS		
KEY PLAN		
RELEASE FOR CONSTRUCTION		
DRAWING TITLE		
BATHROOM 1-13 PRODUCTS LIST		
FBO PROJECT NUMBER	DRAWING SCALE	PHASE
CADD FILE NAME	CADD PLOT SCALE	☐ CONCEPT ☐ 35% ☐ 50% ☐ 90% ☐ 100% ☒ FINAL
LJU_CMR_SECOND_FLOOR_BATHROOM		
DATE April 28, 2026 DRAWN BY Ntouneta, M CHECKED BY PROJECT NUMBER CLASSIFICATION SENSITIVE BUT UNCLASSIFIED		CADD Plot Scale A06