


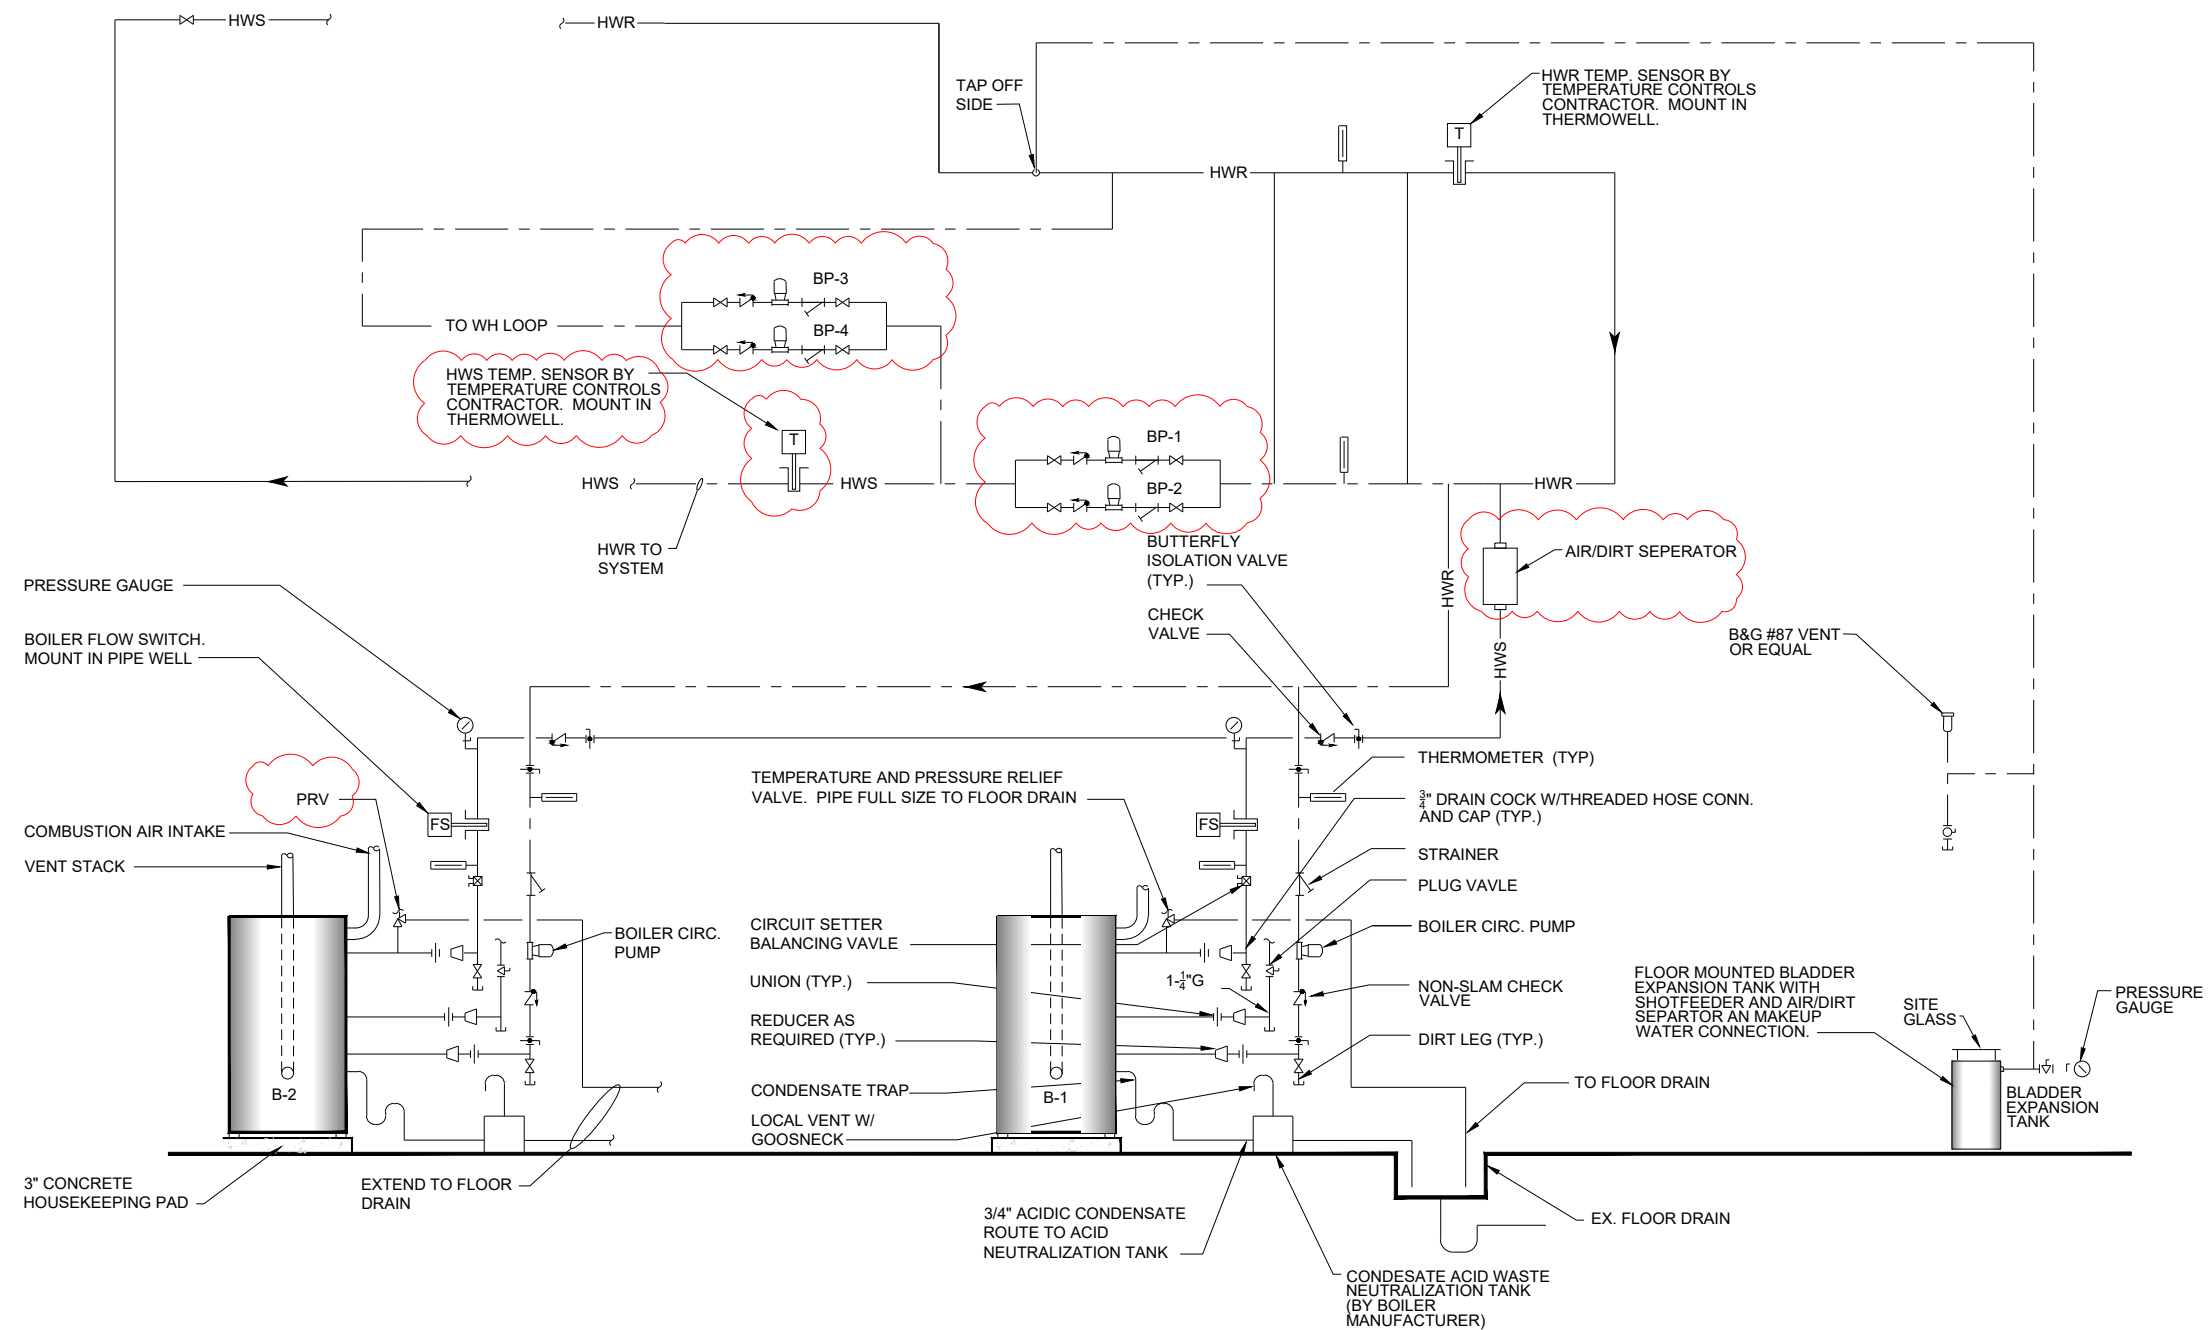

1 HEATING PLANT PIPING DIAGRAM
6 SCALE: N.T.S.

Mark	Date	Description
01	7/23/2025	GENERAL REVISION

Date:	24JUL2025
Scale:	N.T.S.
File:	-
Project Number:	VGLZ 242015
Drawn By:	J. AUSTIN
Designed By:	T. RESH
Checked By:	T. RESH

REPAIR HVAC BLDG 105

NEW HEATING HW BOILERS PIPING & CONTROLS