
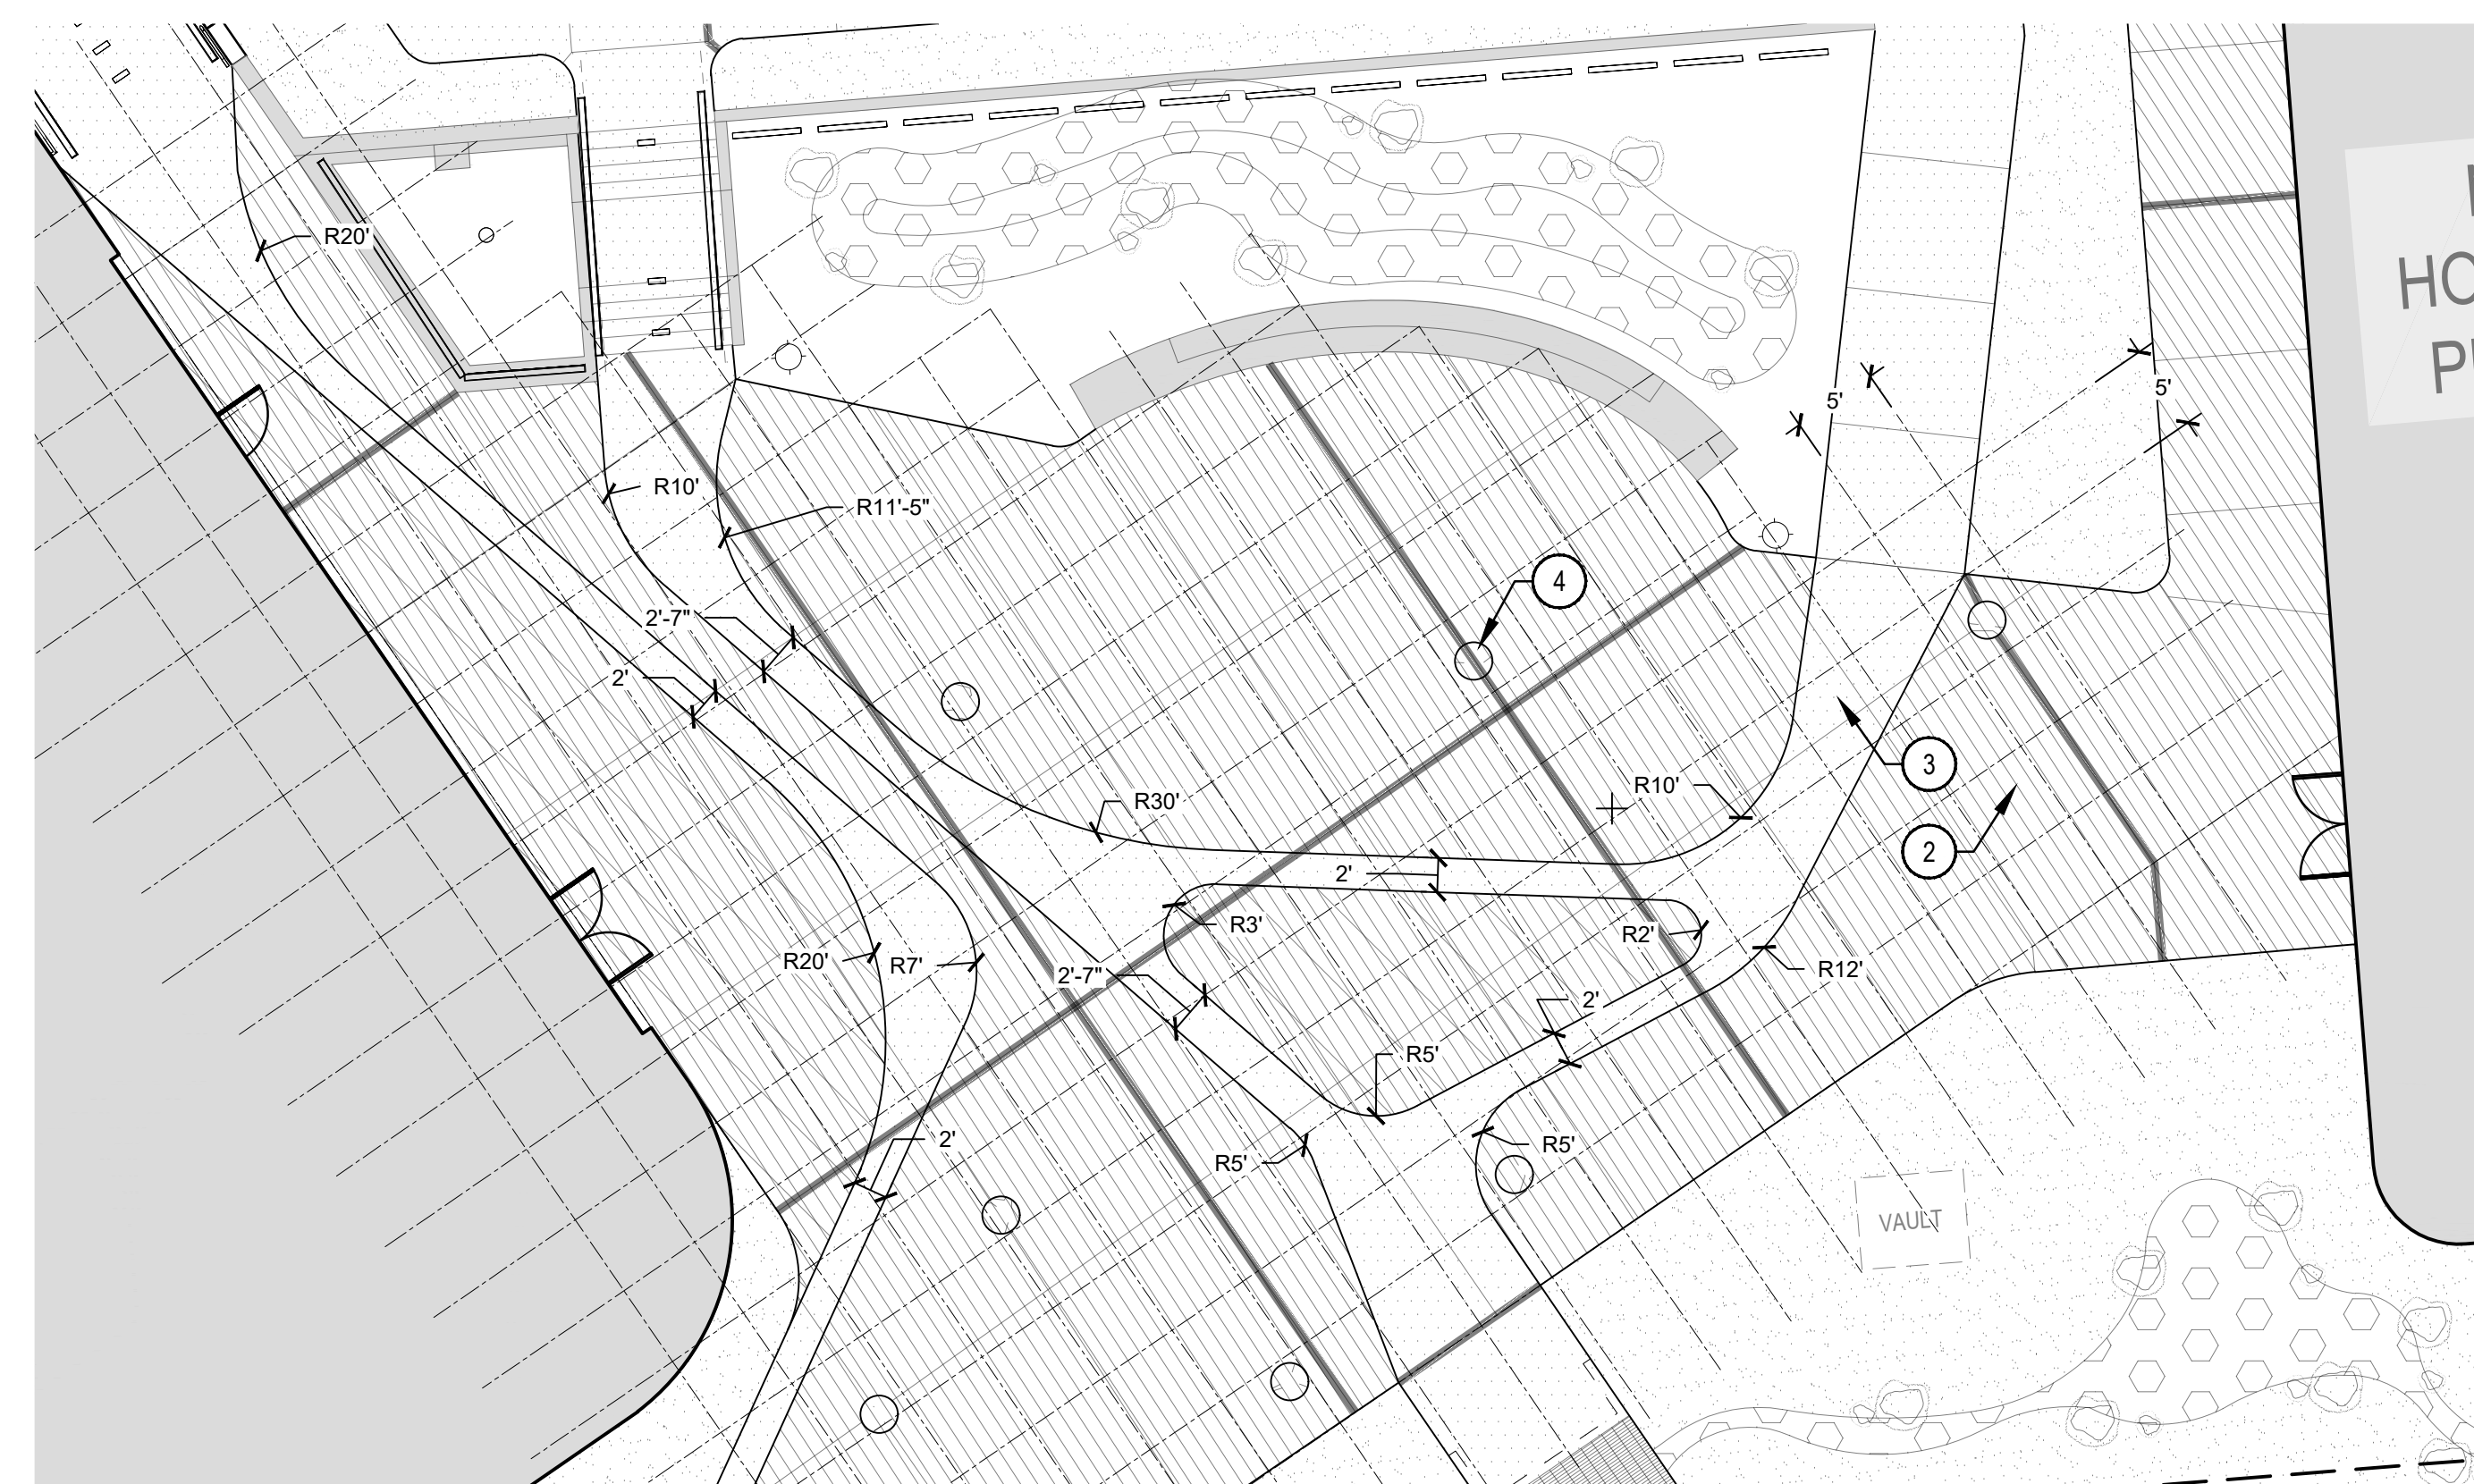
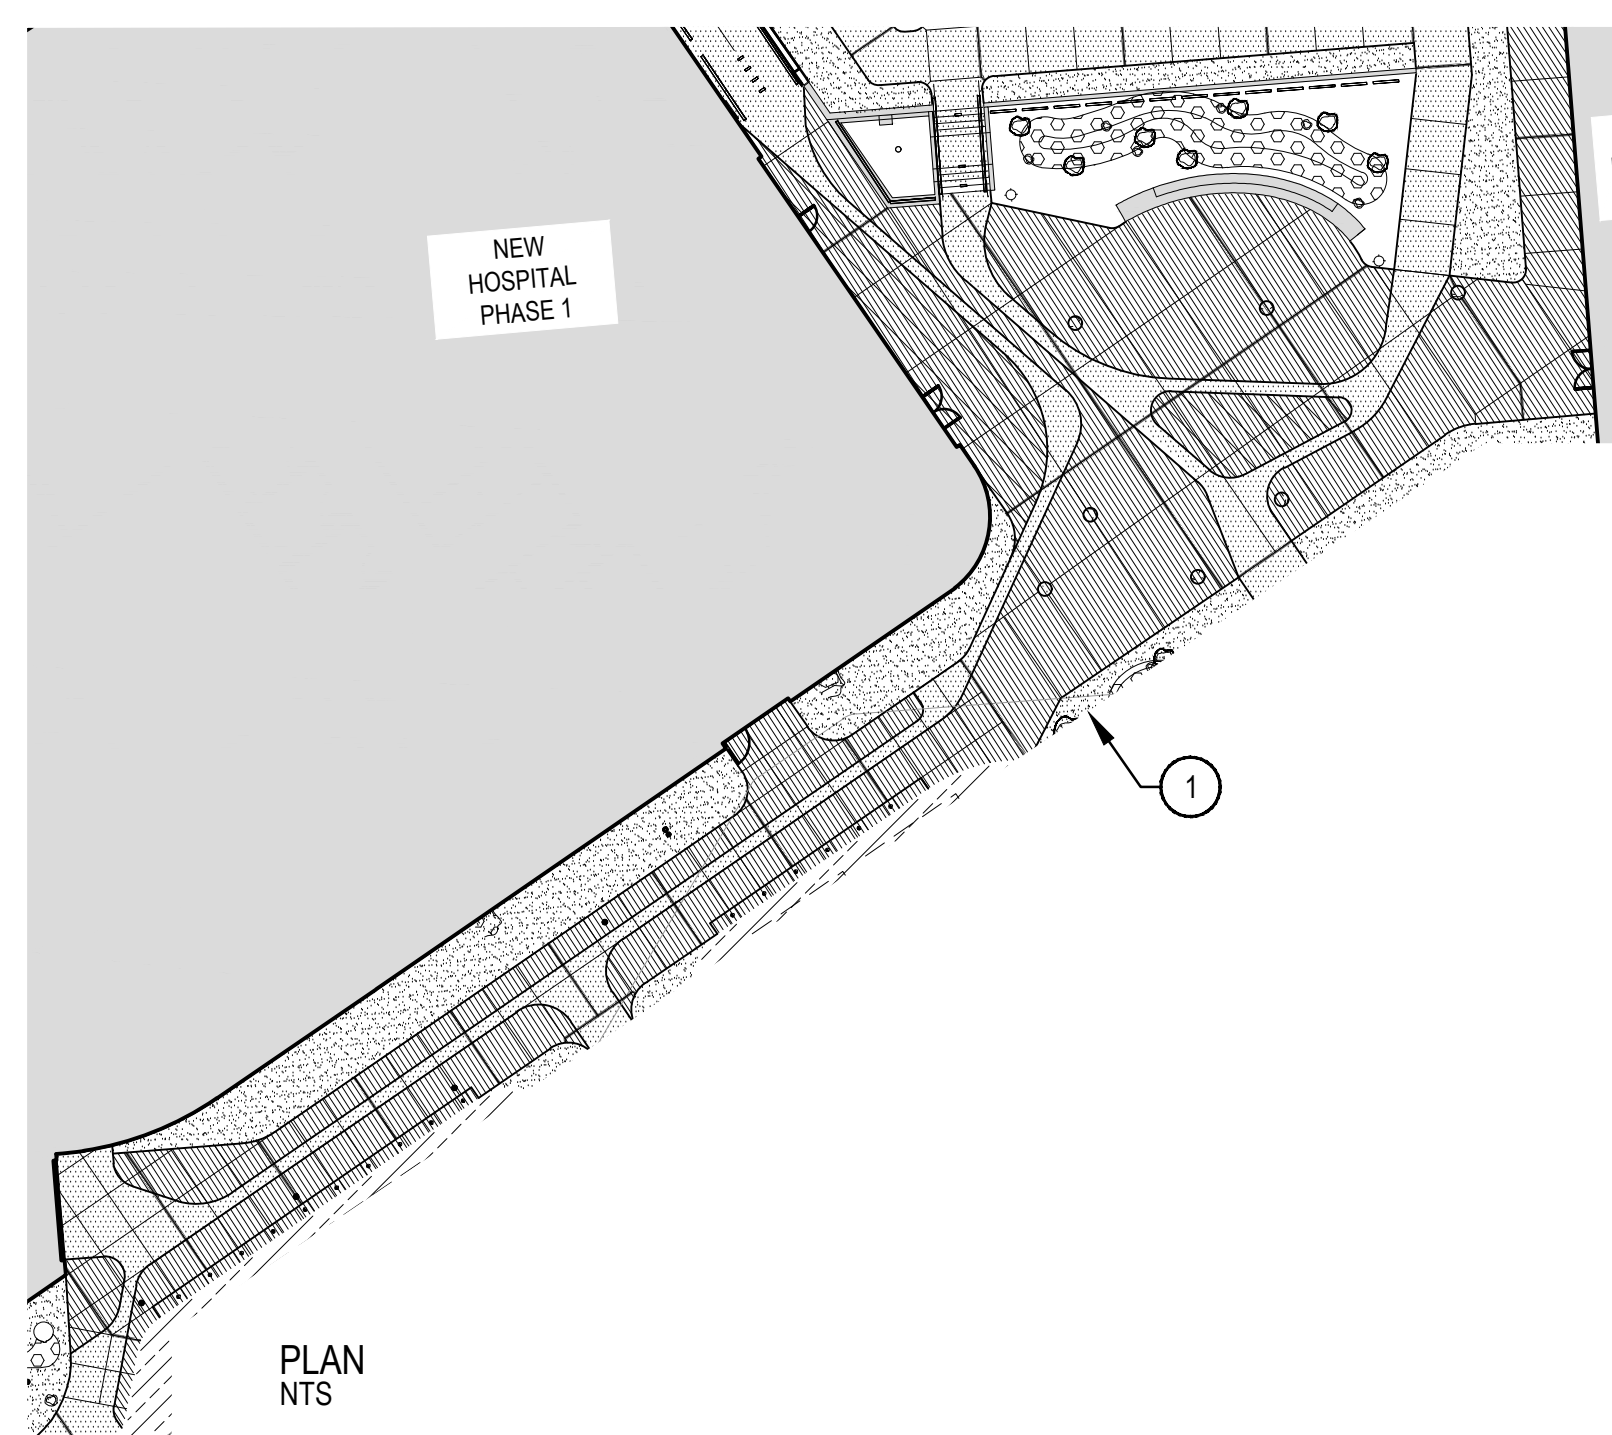
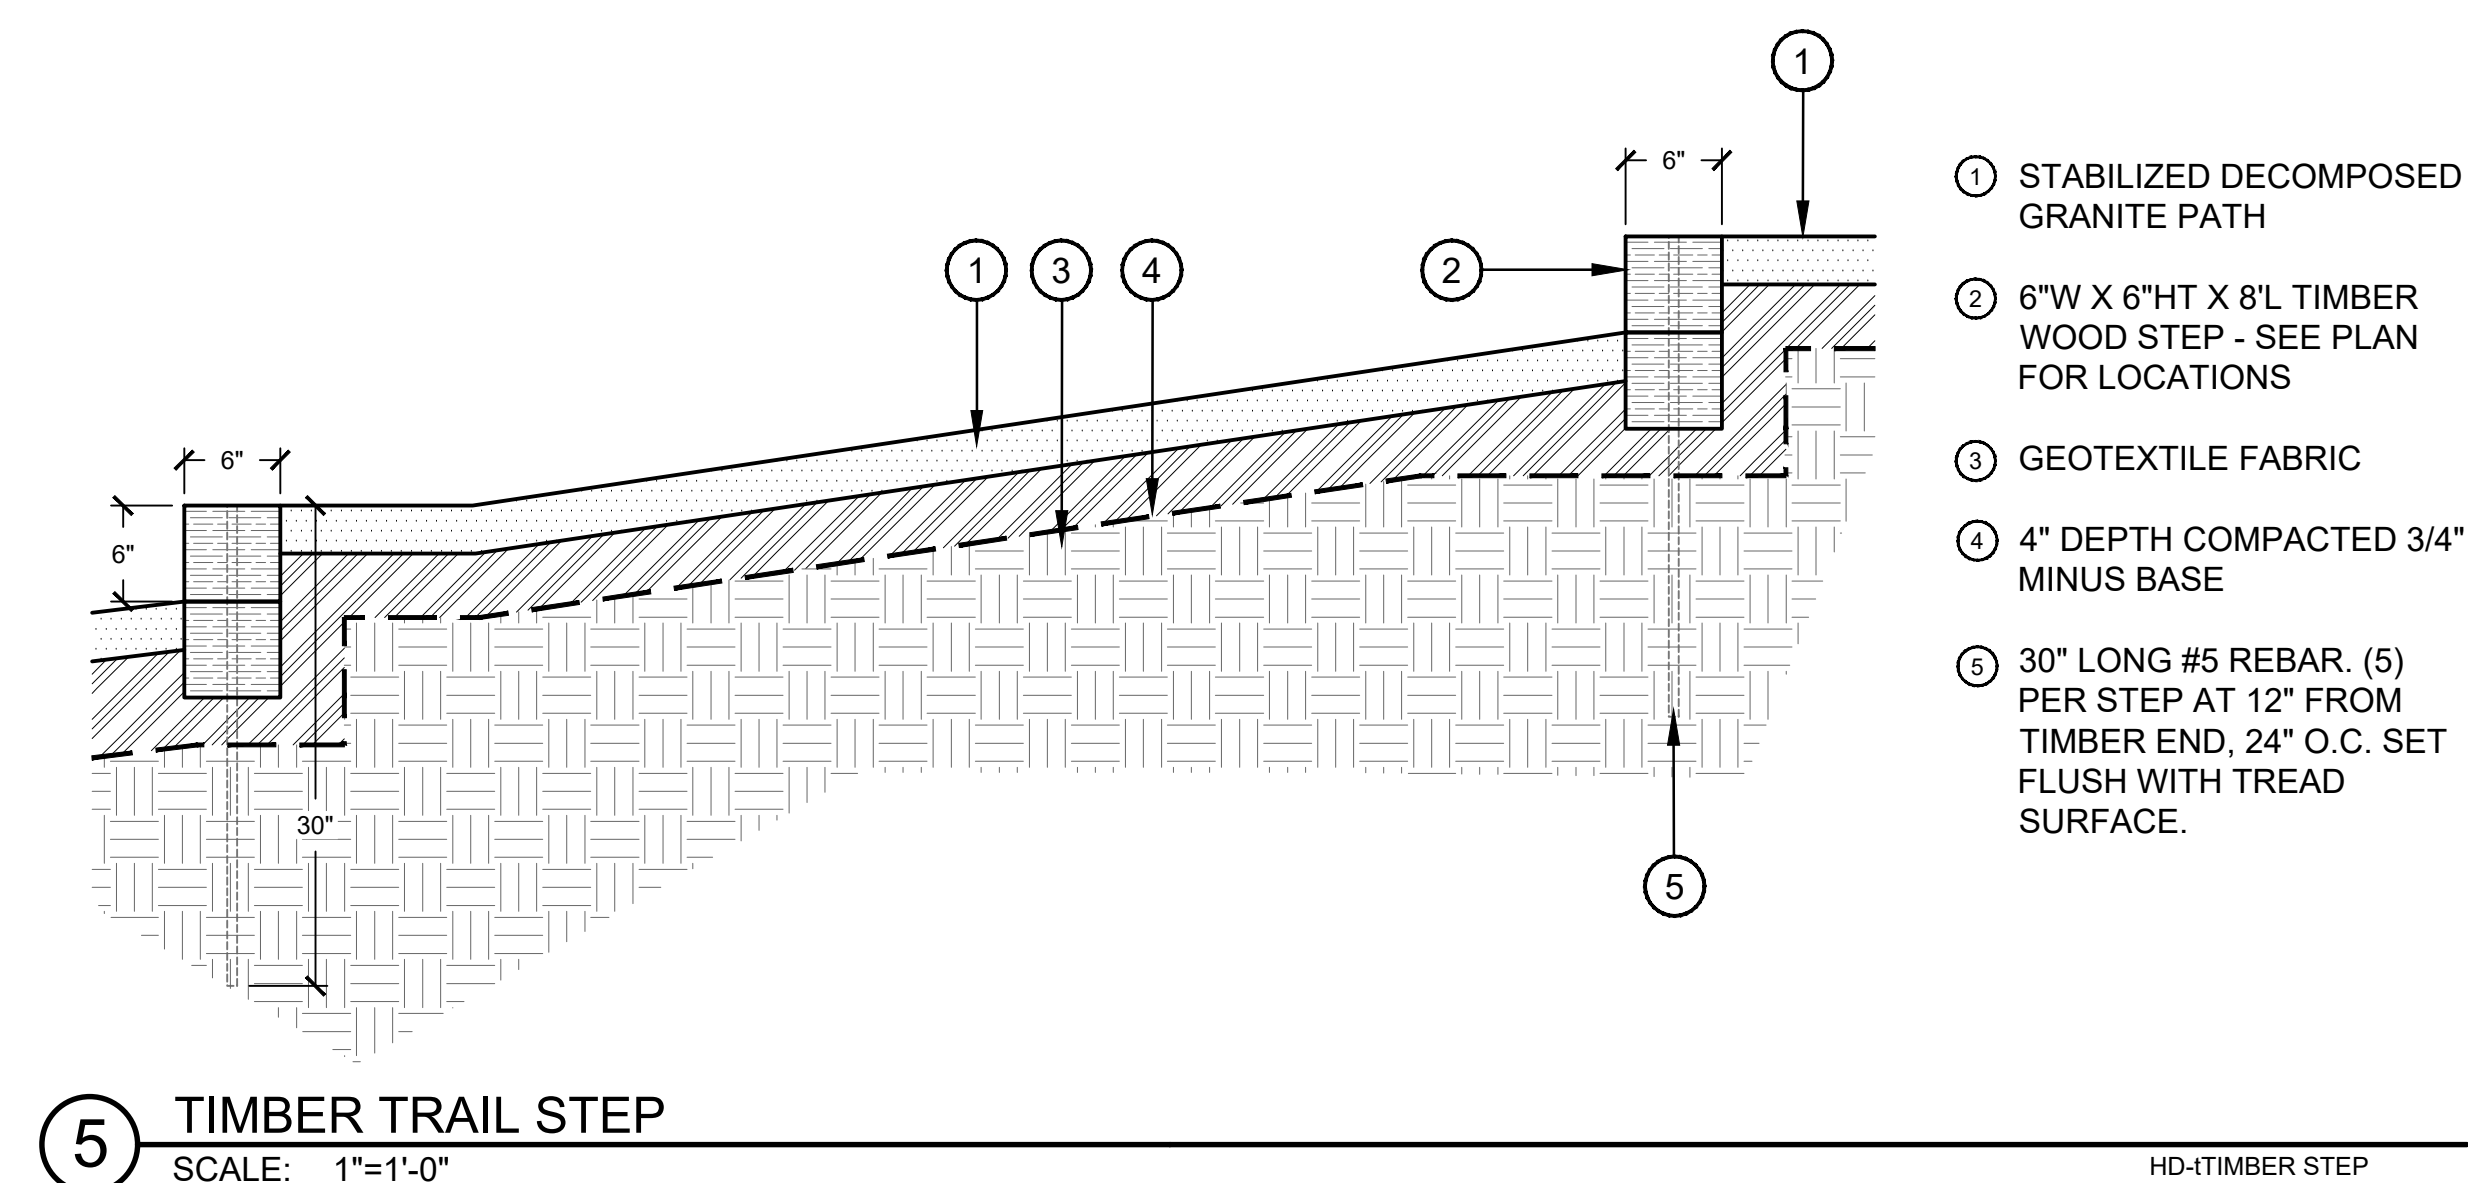
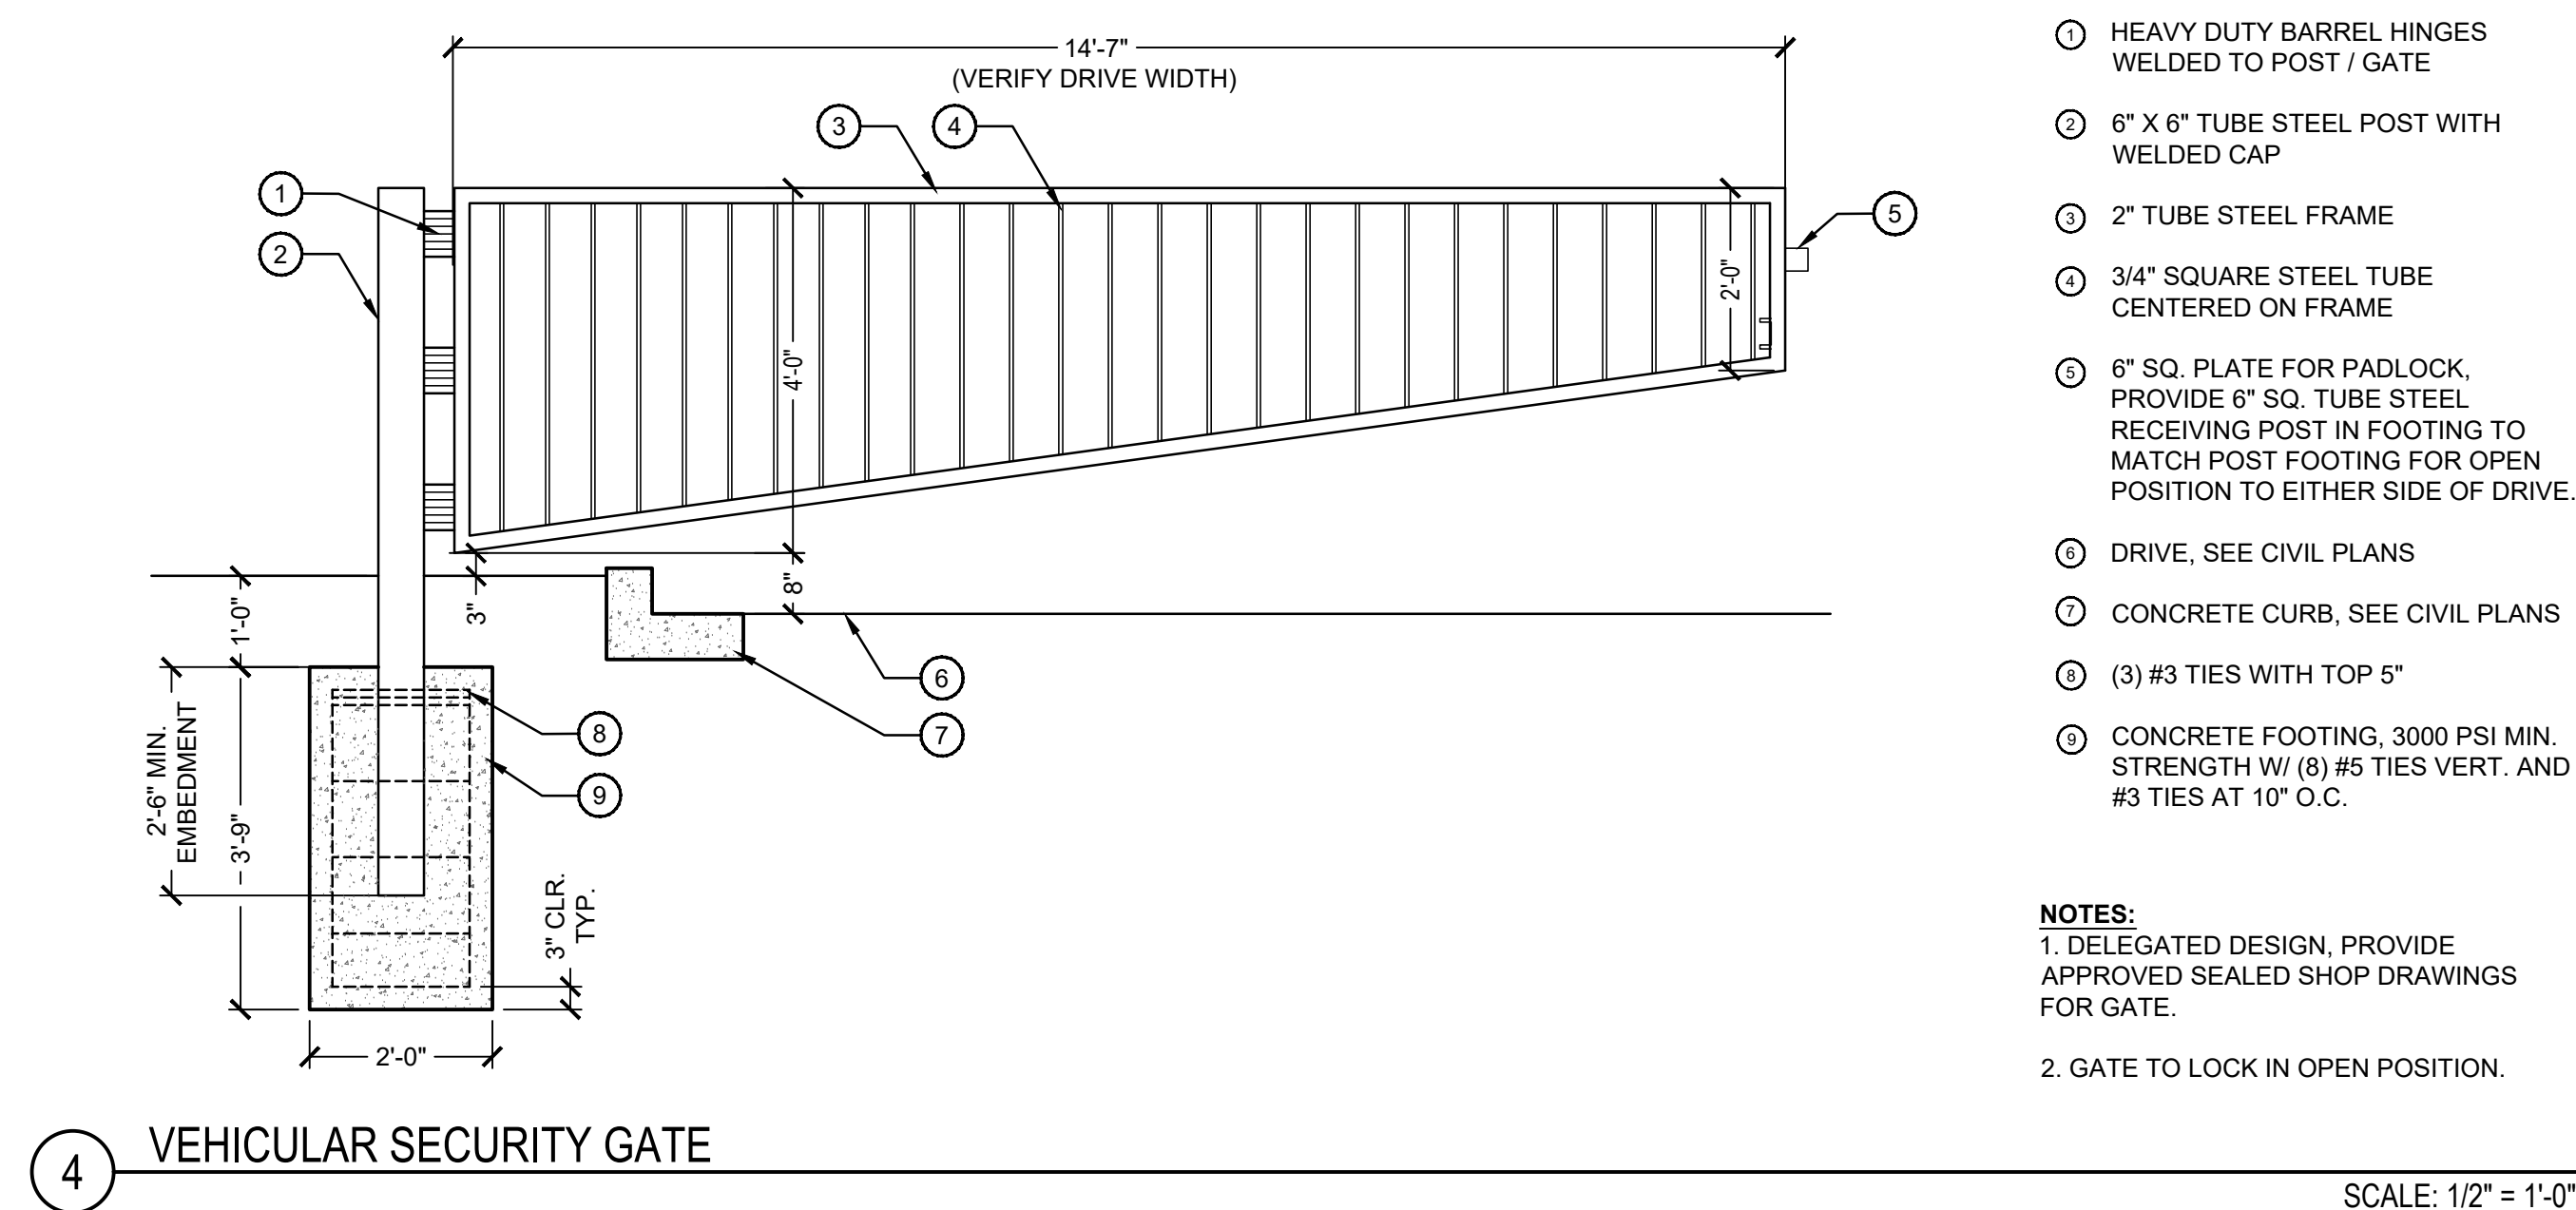
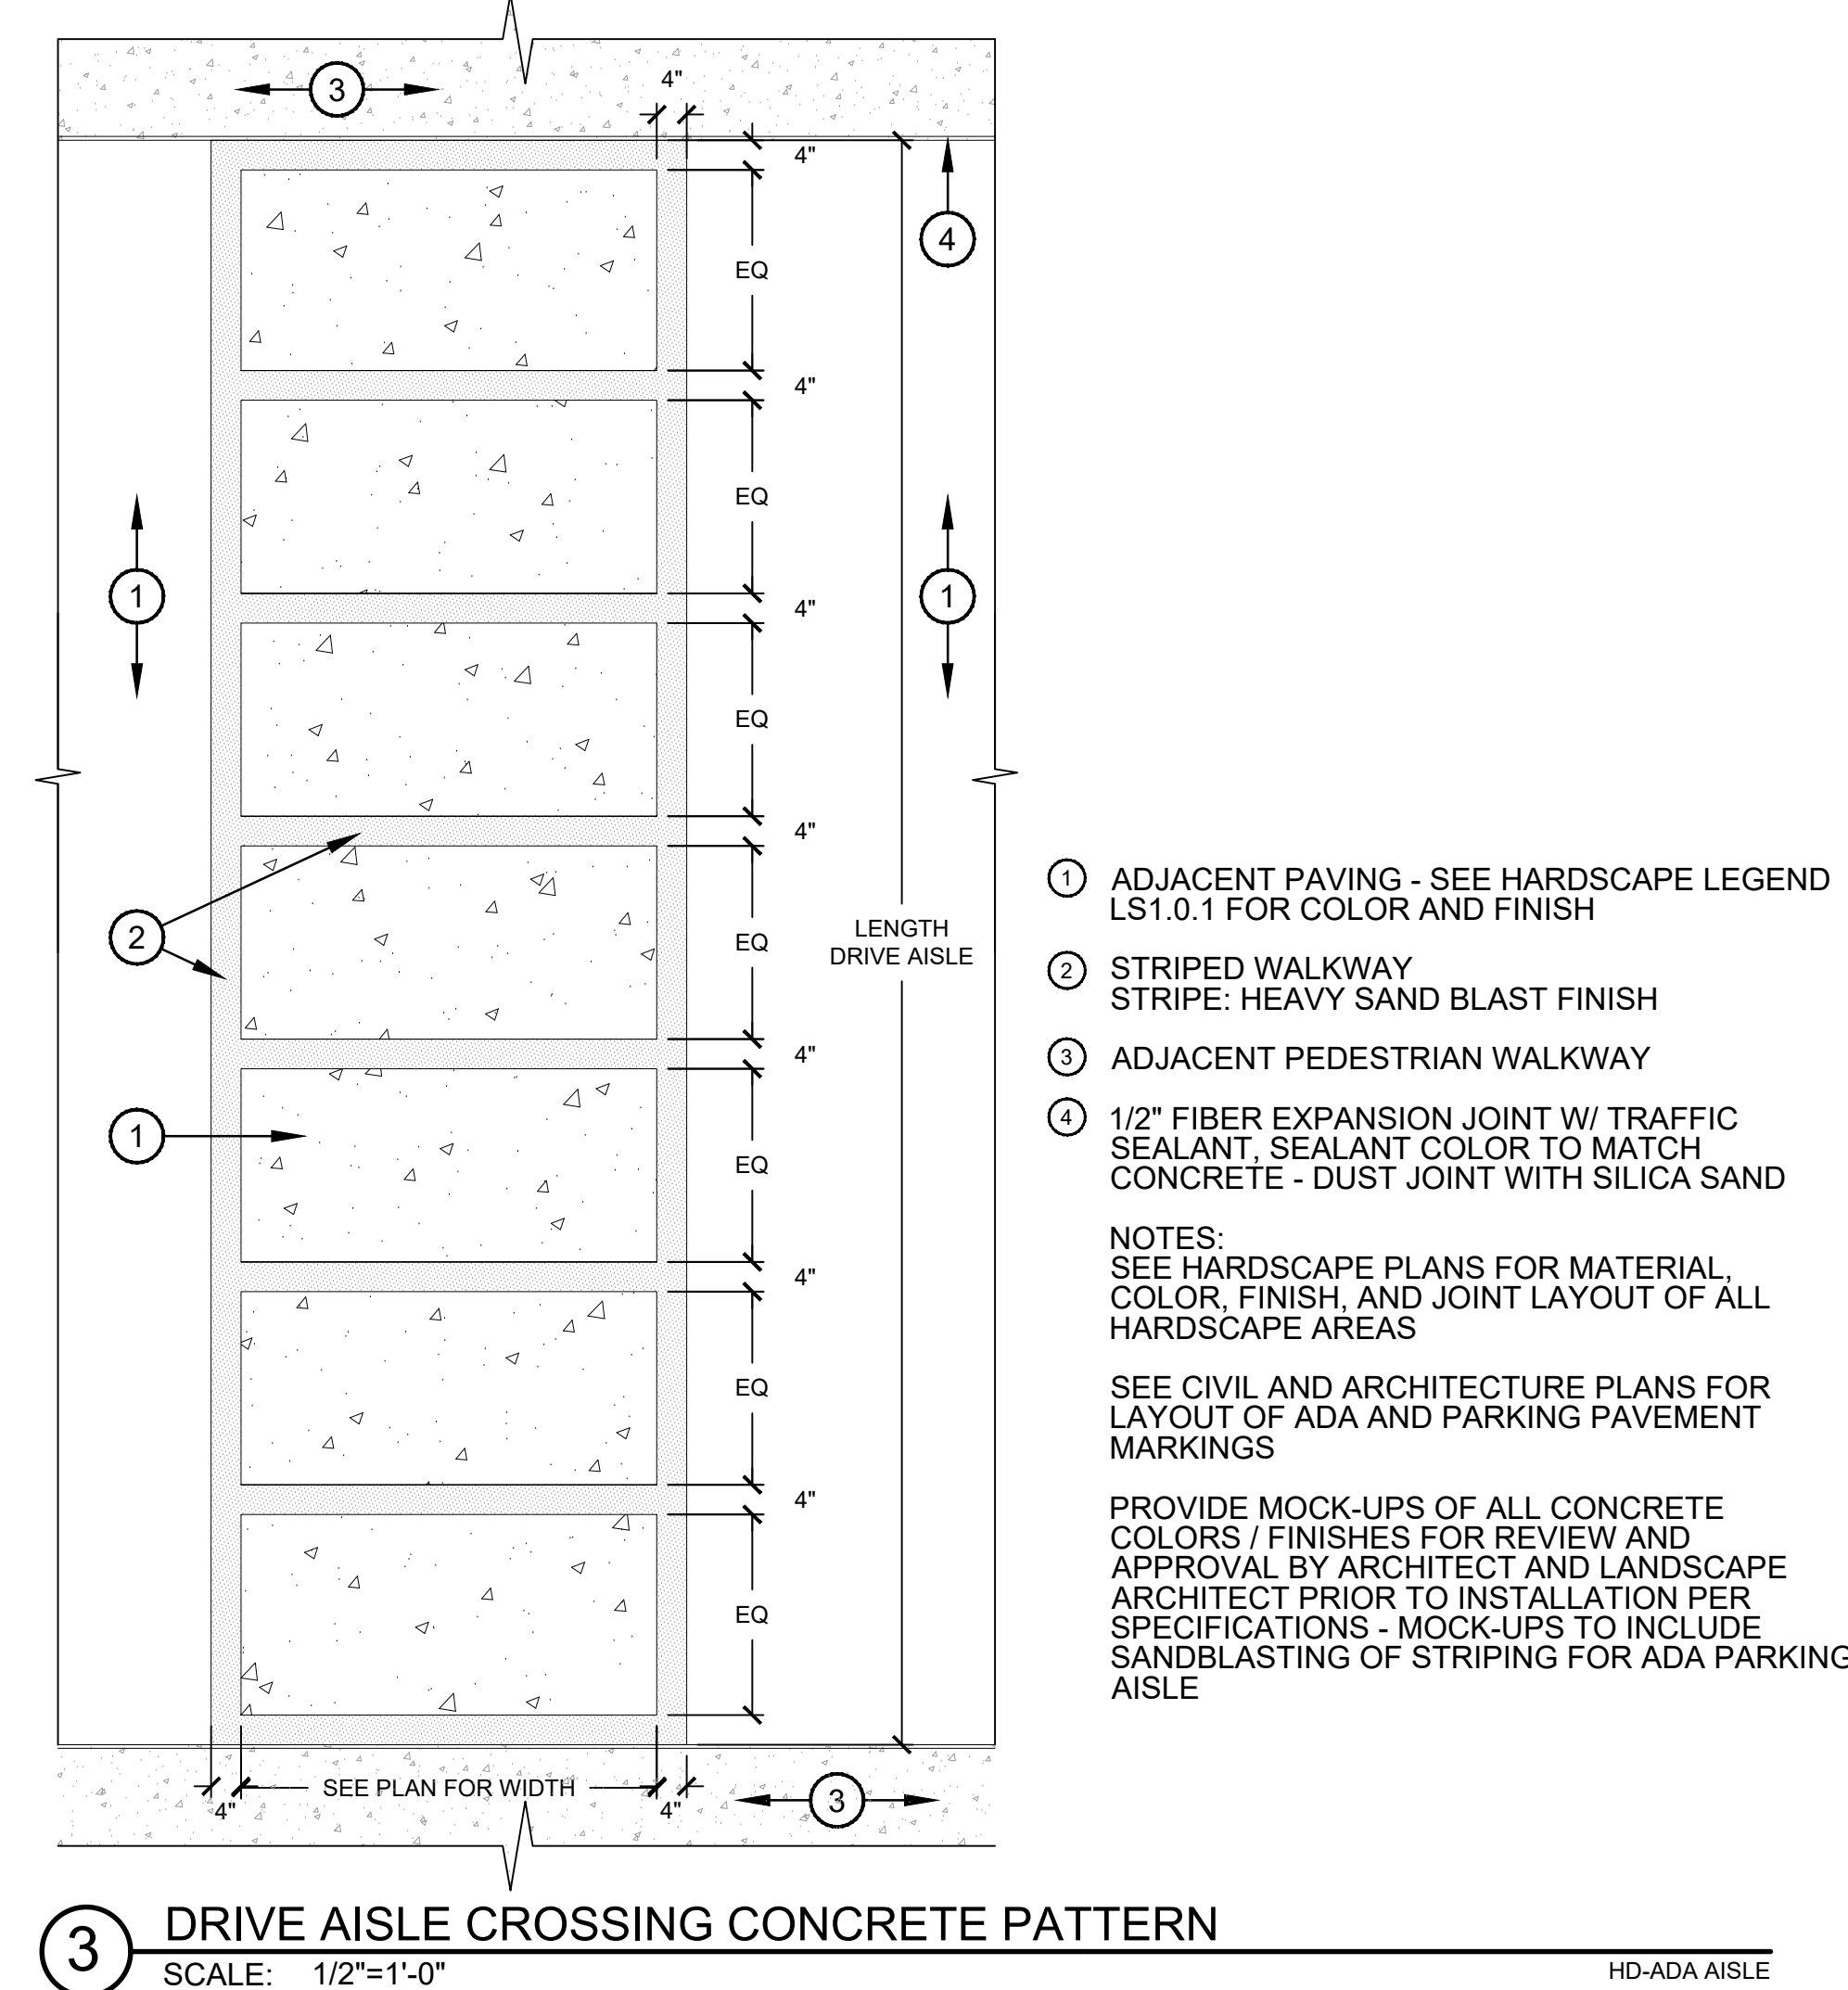
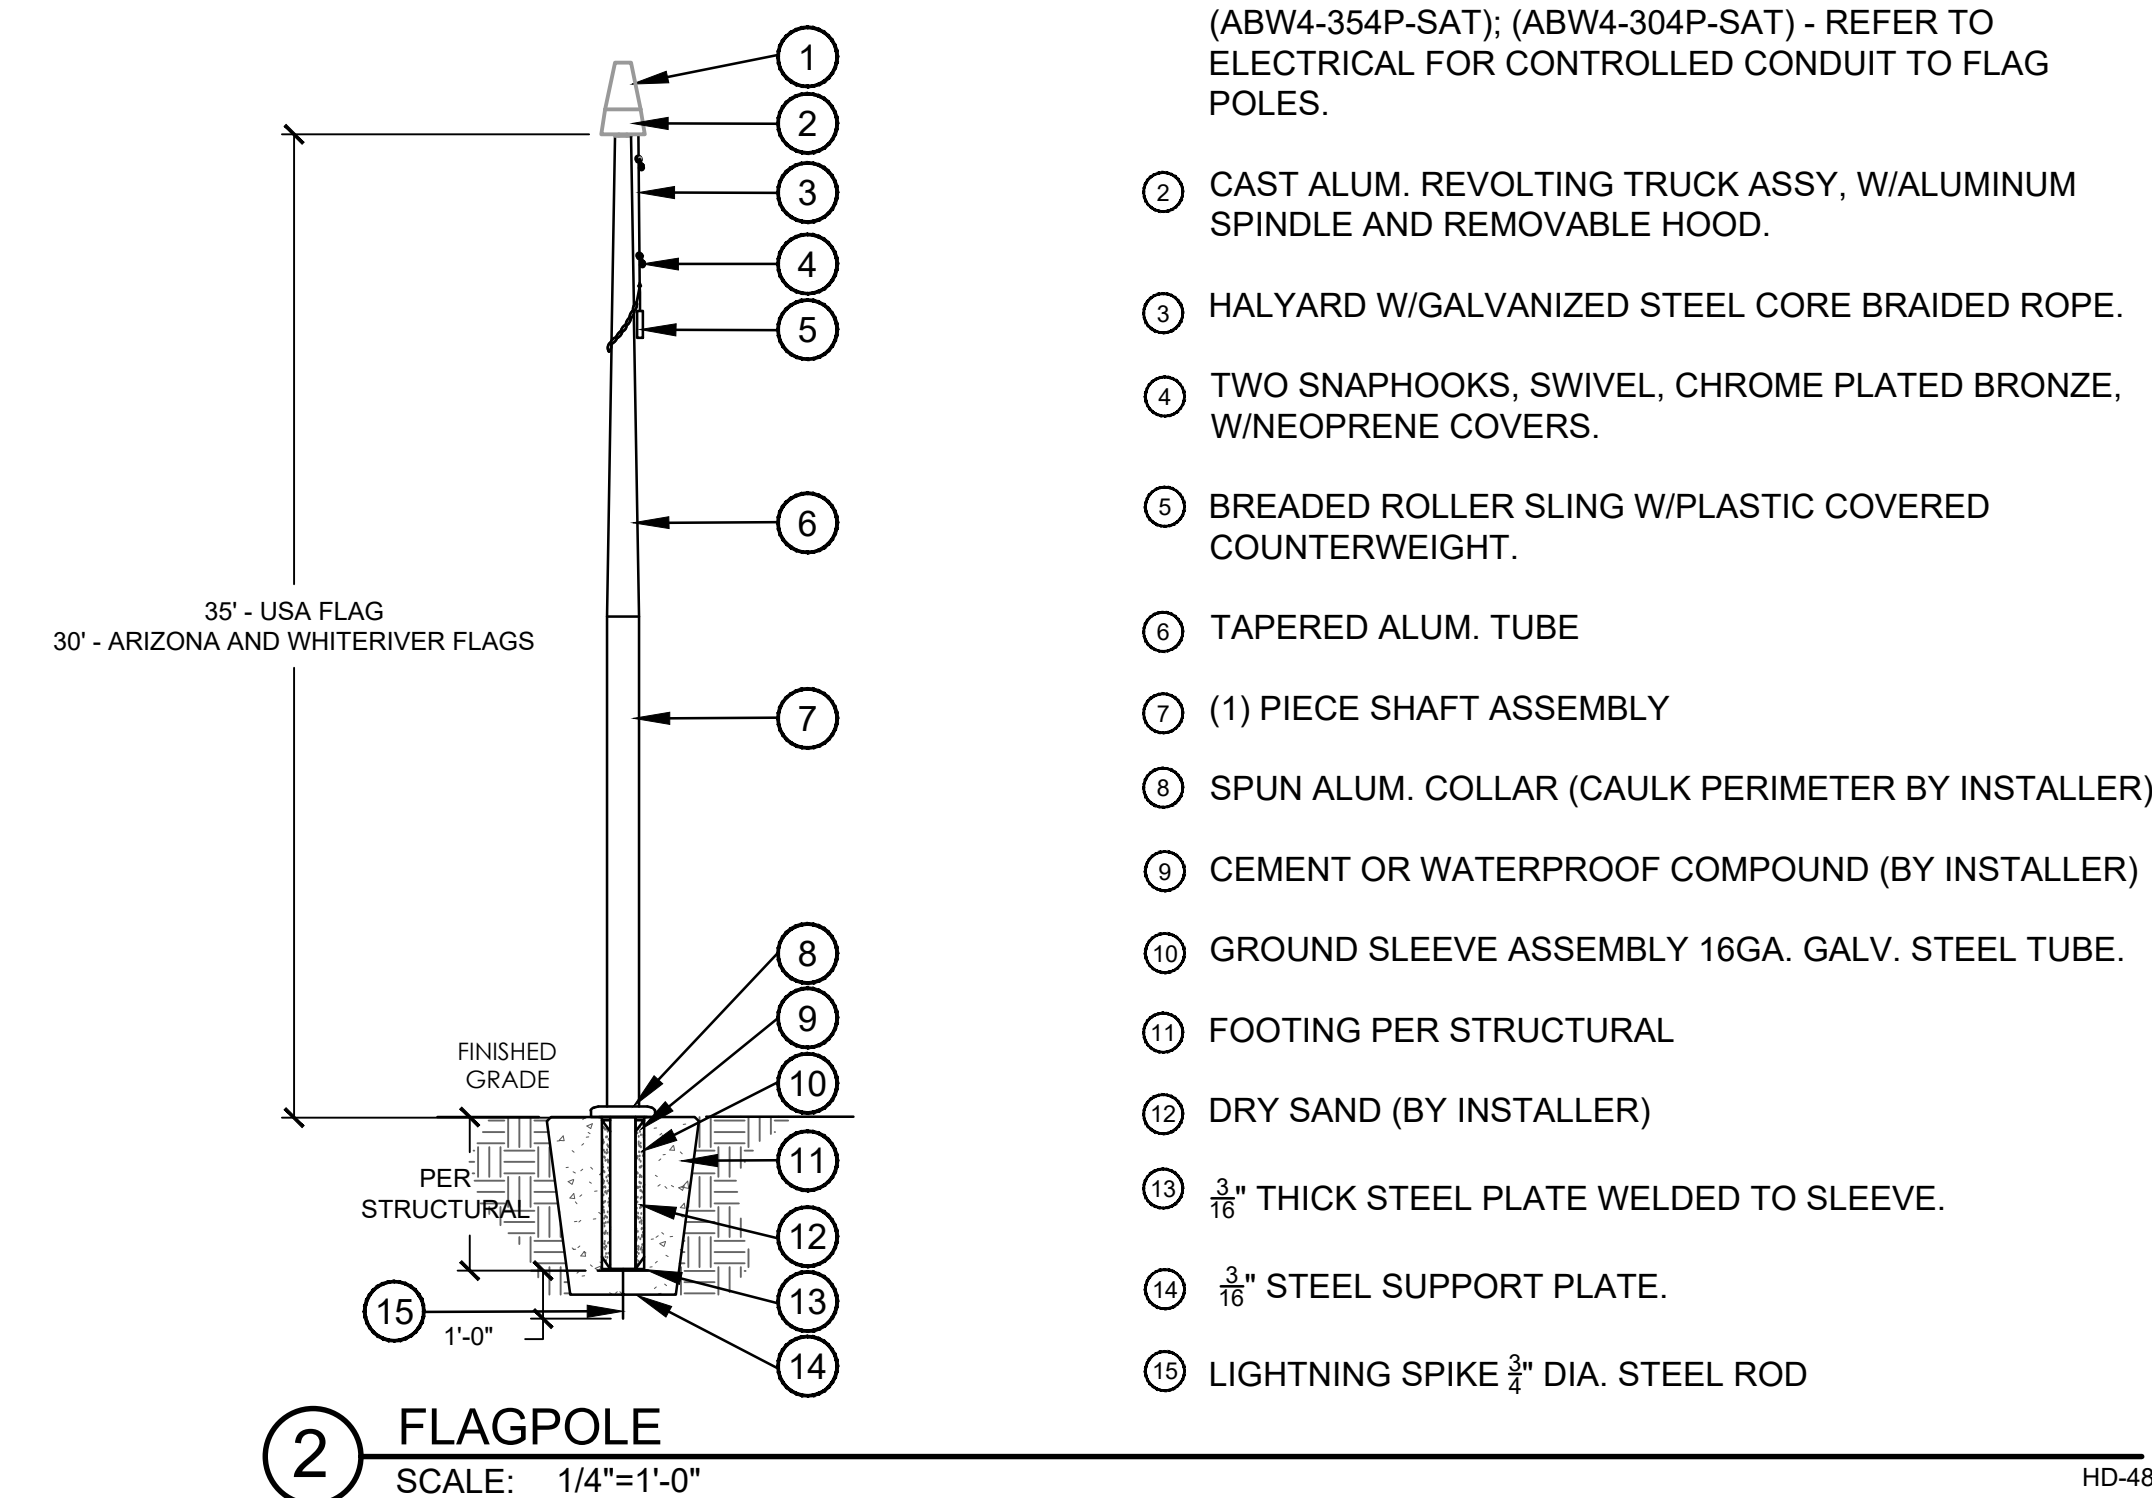


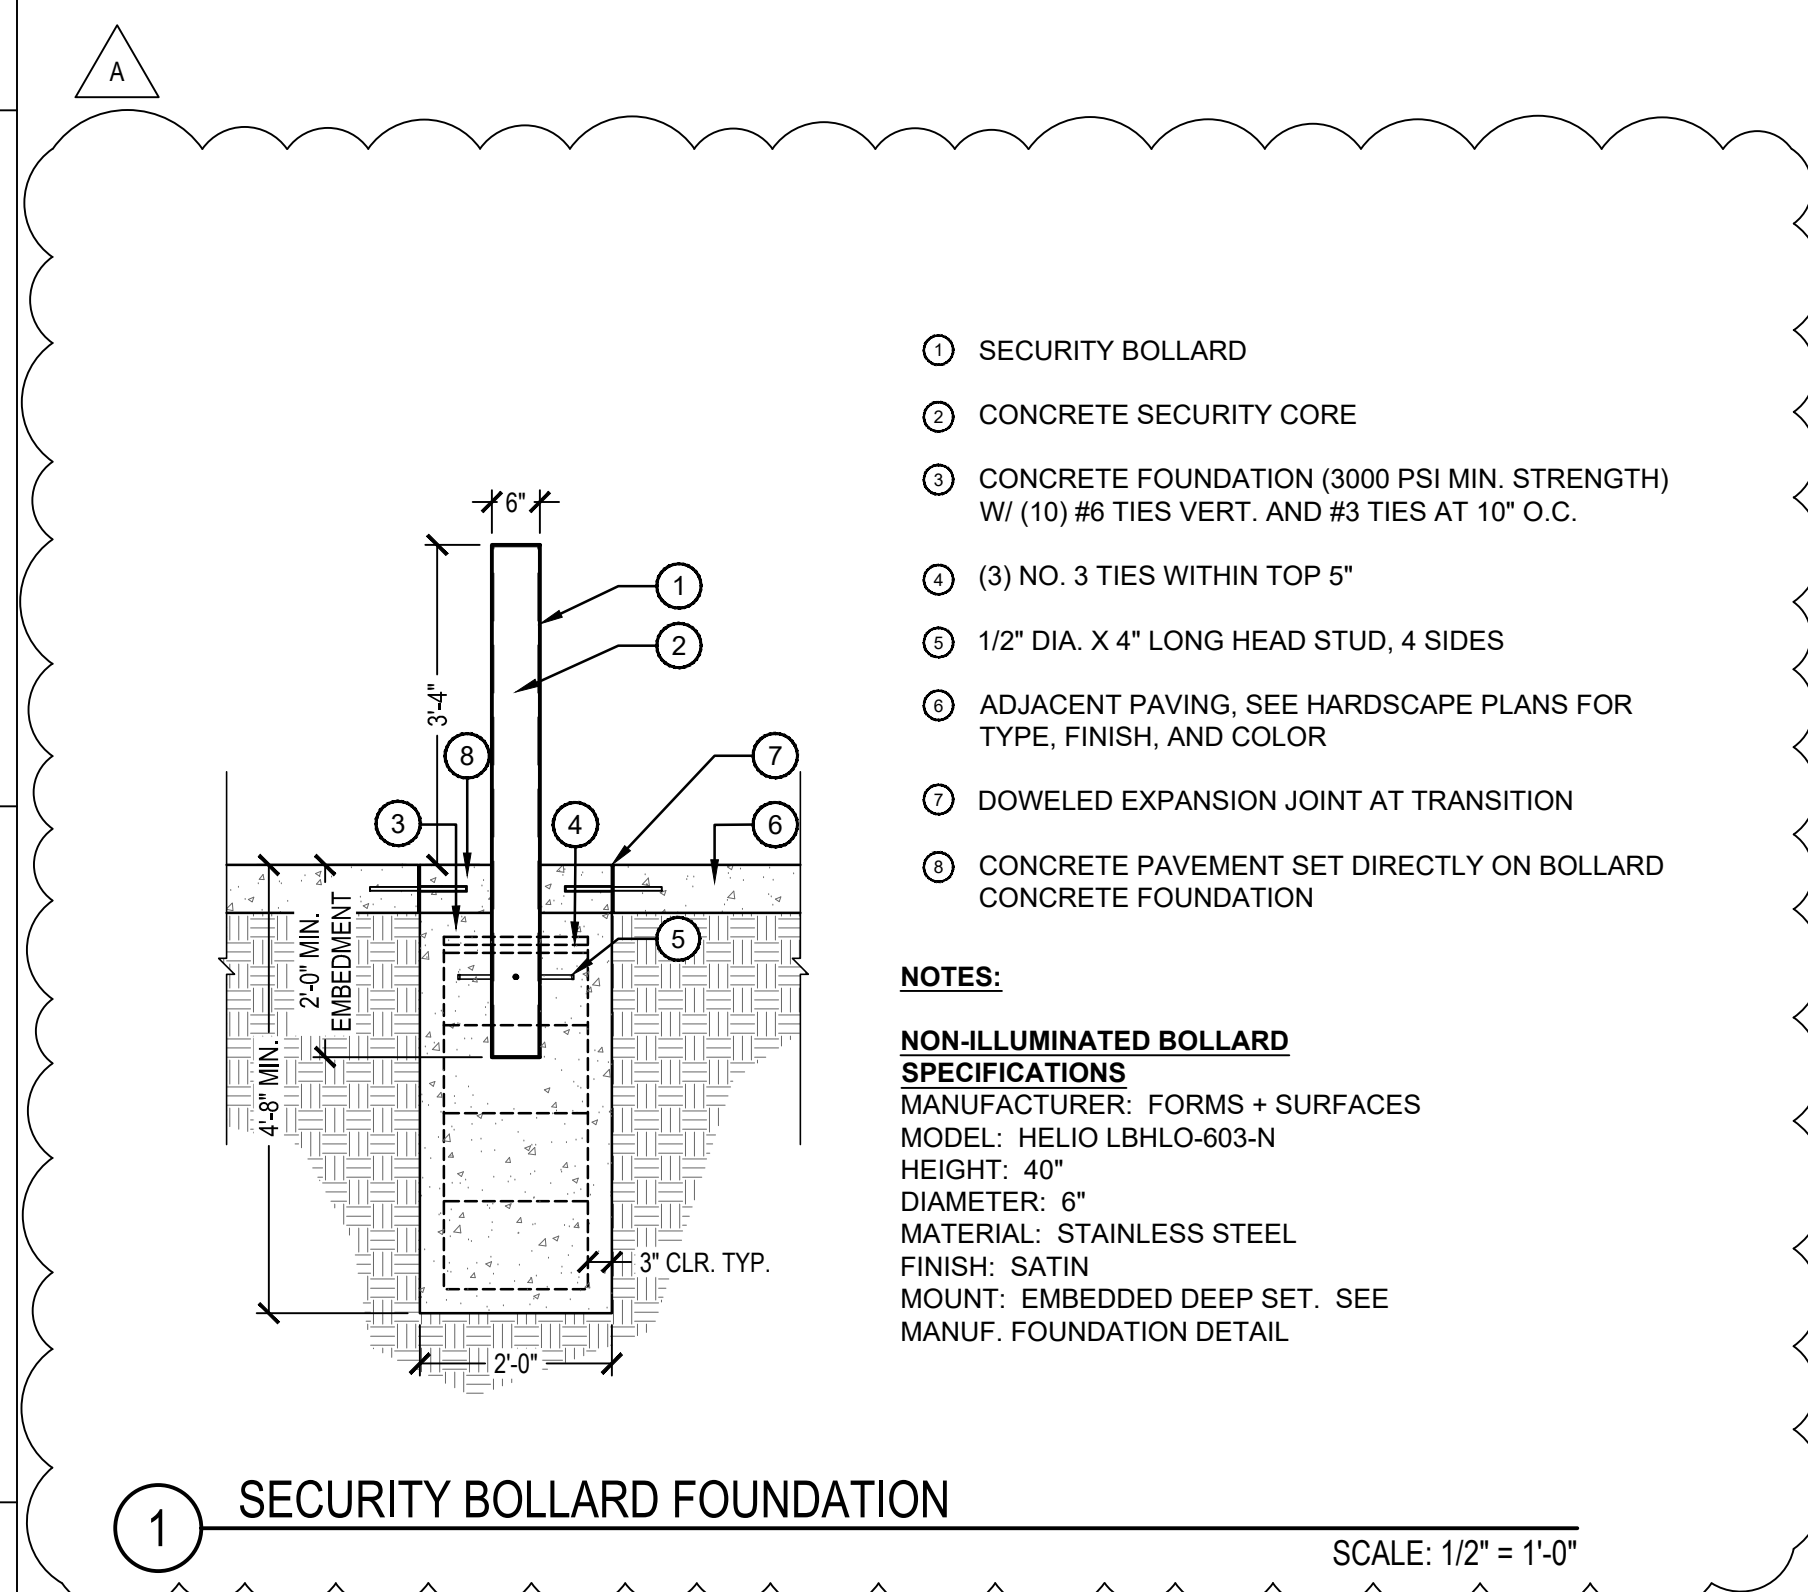

- ① EXTENT OF INTEGRAL COLOR CONCRETE PATTERN AT COURTYARD. OVERLAY 5X5 GRID TO MAP DESIGN LAYOUT. SEE PLAN ENLARGEMENT.
- ② INTEGRAL COLOR CONCRETE: ADOBE WITH TOP CAST 05 FINISH.
- ③ INTEGRAL COLOR CONCRETE: PEBBLE WITH TOP CAST 05 FINISH.
- ④ STEEL COLLAR AT BUILDING COLUMN - SEE ARCHITECTURE DRAWINGS

NOTE:
PROVIDE MOCK-UP FOR REVIEW AND APPROVAL BY LANDSCAPE ARCHITECT.
MOCK-UP TO INCLUDE INTEGRAL COLOR CONCRETE, FINISHES, AND JOINT SAMPLE.

BASED ON PROGRAM OF REQUIREMENTS DATED [03/26/22],
FOR AMENDMENT DATED [02/03/25], AND ON SCHEMATIC
DRAWINGS APPROVED [11/19/24].

SMITHGROUP

455 NORTH THIRD STREET
SUITE 250
PHOENIX, AZ 85004
602.265.2200
smithgroup.com

[illegible]

REGISTERED LANDSCAPE ARCHITECT
 CERTIFICATE NO. 47191
 RICHARD P. JONES
 DATE SIGNED 5.15.2012
 ARIZONA, U.S.A.

EXPIRES: 03/31/28

KEYMAP

SITE DETAILS

Drawn By: MICHAELS Checked By: JONES

PROJECT NUMBER
CD
SHEET NUMBER
LS5.0.2