

Controlled Unclassified Information (CUI) Only

Project: (UHHZ143000R1) Repair/Renovate Aircraft Corrosion Control Facility BLDG 59 Review: Bidder Inquiry

Concur | Other

Type: Keyword: Discipline:

Viewing 4 of 4 Items

Status

This inquiry has not yet been evaluated.

Inquiry ID: 11307883(display only)

- b. Comment Classification: UNCLASSIFIED (U)
- c. Design Discipline: Structural
- d. Spec Section: N/A
- e. Drawing Sheet/Detail: SD107 N/A
- f. Inquiry Text: **Note DS1 and DS8 both point towards the same slab area. Please disgnate the extent of DS8 which is the 8" slab.**

Submitted by Matthew Bosman (phone: 6129161786) matt.bosman@richardgroup.com on Apr 23 2025 06:08 PM

Add Evaluation 1

- a. Status (req.) ☒ Concur ☐ Non-concur ☒ For information only ☐ Check and resolve
- b. Discussion (req.) (0)

Refer to the attached sketch clarifying the extents of the 8" slab on grade.


- c. Include Amendment (req.) ☐ Yes ☒ No
- d. Potential Scope Impact (opt.) ☐ Yes ☒ No
- e. Potential Cost Impact (opt.) ☐ Yes ☒ No
- f. Potential Schedule Impact (opt.) ☐ Yes ☒ No
- g. Attachment (opt.) No file chosen

Viewing 4 of 4 Items

Next >

Last>>

Controlled Unclassified Information (CUI) Only
Patent 11/892,984 ProjNet property of ERDC since 2004.

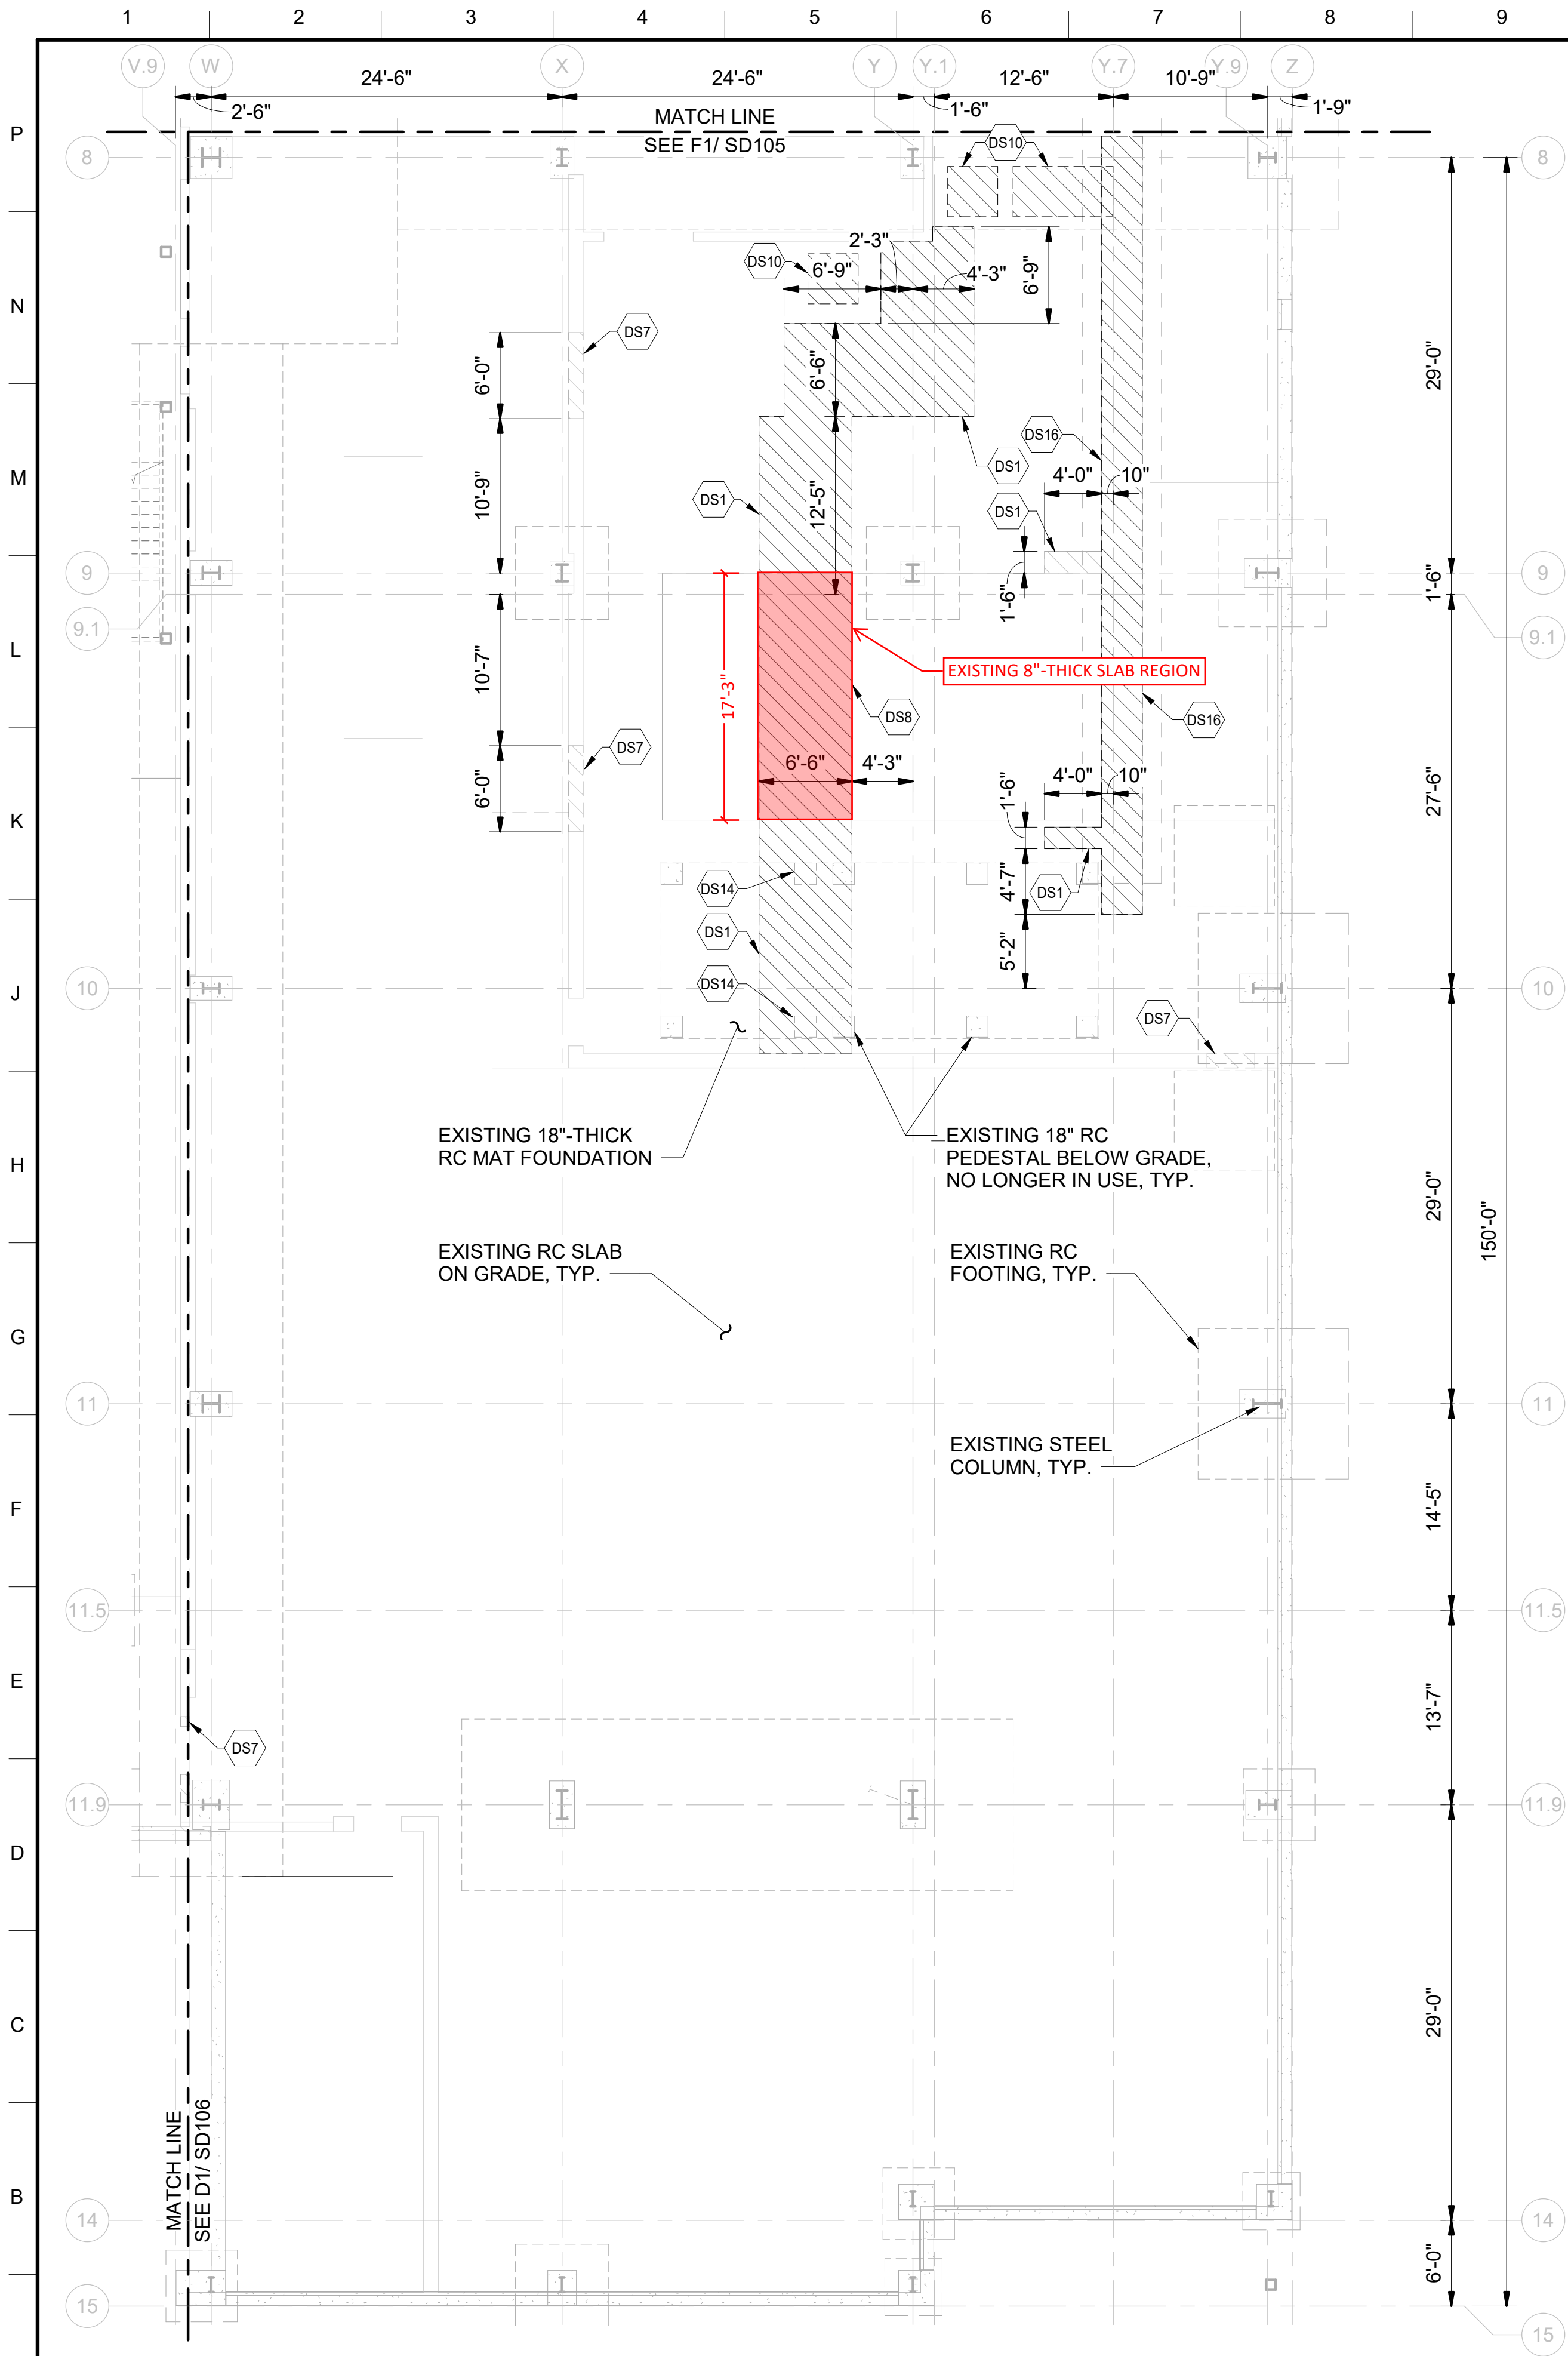

A1 FOUNDATION DEMOLITION PLAN - AREA D8
SCALE: 1/8" = 1'-0"

LEGEND


- EXISTING STRUCTURE TO BE REMOVED
- EXISTING STRUCTURE TO REMAIN
- EXISTING FOOTING
- EXISTING TRENCH GRATE DEMOLITION CONDITION

GENERAL NOTES


- ALL EXISTING CONDITIONS ARE SHOWN PER THE EXISTING BUILDING DRAWING SETS AND NON-DESTRUCTIVE SITE INVESTIGATIONS. GENERAL CONTRACTOR SHALL VERIFY ALL DIMENSIONS AND CONDITIONS PRIOR TO DEMOLITION AND CONSTRUCTION.
- CONTRACTOR IS RESPONSIBLE FOR DETERMINING NEED FOR AND PROVIDING ALL REQUIRED TEMPORARY SHORING AND BRACING DURING DEMOLITION AND CONSTRUCTION.
- UNLESS OTHERWISE NOTED, EXISTING FOOTING FOUNDATION ELEMENTS SHALL NOT BE DAMAGED OR DISTURBED.
- SUBSTANCE-SPECIFIC DUST (SSD) CONTAINING LEAD, HEXAVALENT CHROMIUM, CADMIUM, BERYLLIUM, AND SIMILAR HEAVY METALS IS TO BE ASSUMED PRESENT ON SURFACES THROUGHOUT THE BUILDING, INCLUDING WITHIN THE EXISTING TRENCHES. REFER TO THE A-003 HAZARDOUS MATERIALS GENERAL NOTES FOR ADDITIONAL INFORMATION.

SHEET KEYNOTES

- DS1 DEMOLISH EXISTING 6-1/2"-THICK (+/- 1") RC SLAB ON GRADE. DO NOT DAMAGE EXISTING COLUMN OR WALL FOOTINGS.
- DS7 SELECTIVELY DEMOLISH EXISTING CMU WALL FOR NEW OPENING. SEE S-502 FOR LINTEL DETAIL.
- DS8 DEMOLISH EXISTING 8"-THICK (+/- 1") RC SLAB ON GRADE. DO NOT DAMAGE EXISTING COLUMN OR WALL FOOTINGS.
- DS10 DEMOLISH EXISTING CONCRETE PADS FLUSH TO TOP OF EXISTING RC SLAB ON GRADE.
- DS14 DEMOLISH EXISTING 18" RC PEDESTAL BELOW GRADE NO LONGER IN USE.
- DS16 DEMOLISH EXISTING TRENCH COVER PLATE AND METAL GRATING. REMOVE EXISTING PIPING WITHIN TRENCH. SEE GENERAL NOTES REGARDING HEAVY METAL CONTAMINATION.

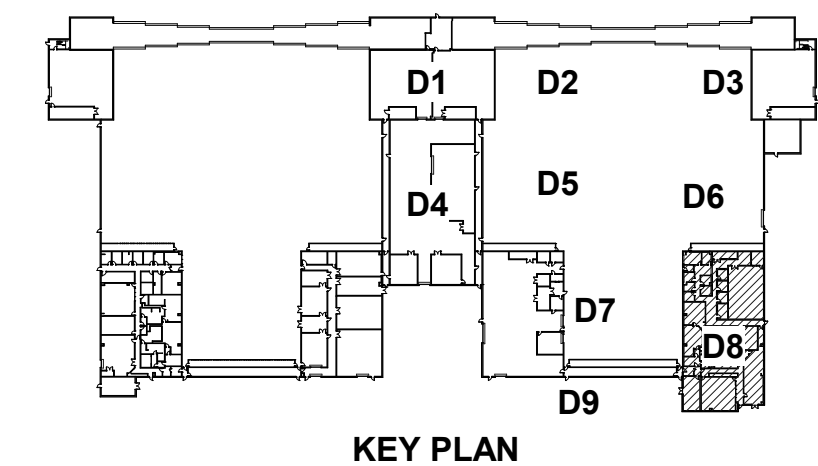


PLAN NORTH

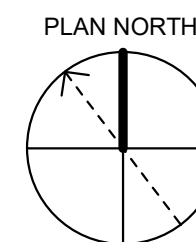

SCALE: 1/8"=1'-0"

GRAPHIC SCALE

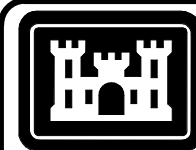

US Army Corps
of Engineers®

MARK	DESCRIPTION	DATE

DESIGNED BY: P. MURREN	ISSUE DATE: 11/20/2024	SOLICITATION NO.: W912HN-25-B-4002
DRAWN BY: P. MURREN	CHECKED BY: E. WIETERS	CONTRACT NO.:
SUBMITTED BY: CEMS ENGINEERING	FILE NAME: ANSI.D	CATEGORY CODE: 211-159-04
US ARMY CORPS OF ENGINEERS 100 WEST OGLETHORPE AVENUE SAVANNAH DISTRICT SAVANNAH, GEORGIA		
CEMS RS&H A JOINT VENTURE		

ROBINS AFB, GA REPAIR/RENOVATE AIRCRAFT CORROSION CONTROL FACILITY BLDG 59 PROJECT NUMBER: UHHZ143000R1	FOUNDATION DEMOLITION PLAN - AREA D8
--	--------------------------------------

SHEET ID
SD107

READY TO ADVERTISE (RTA)