


FILE NAME: \$(getvar, "dwgprefix")\$(getvar, "dwgname") LAYOUT NAME: \$(GETVAR,"CTAB") PLOTTED:\$(etime, 0, %DD%) MONTH DD", YYYY - HAMam/pm) USER: \$(GETVAR,"LOGNAME")

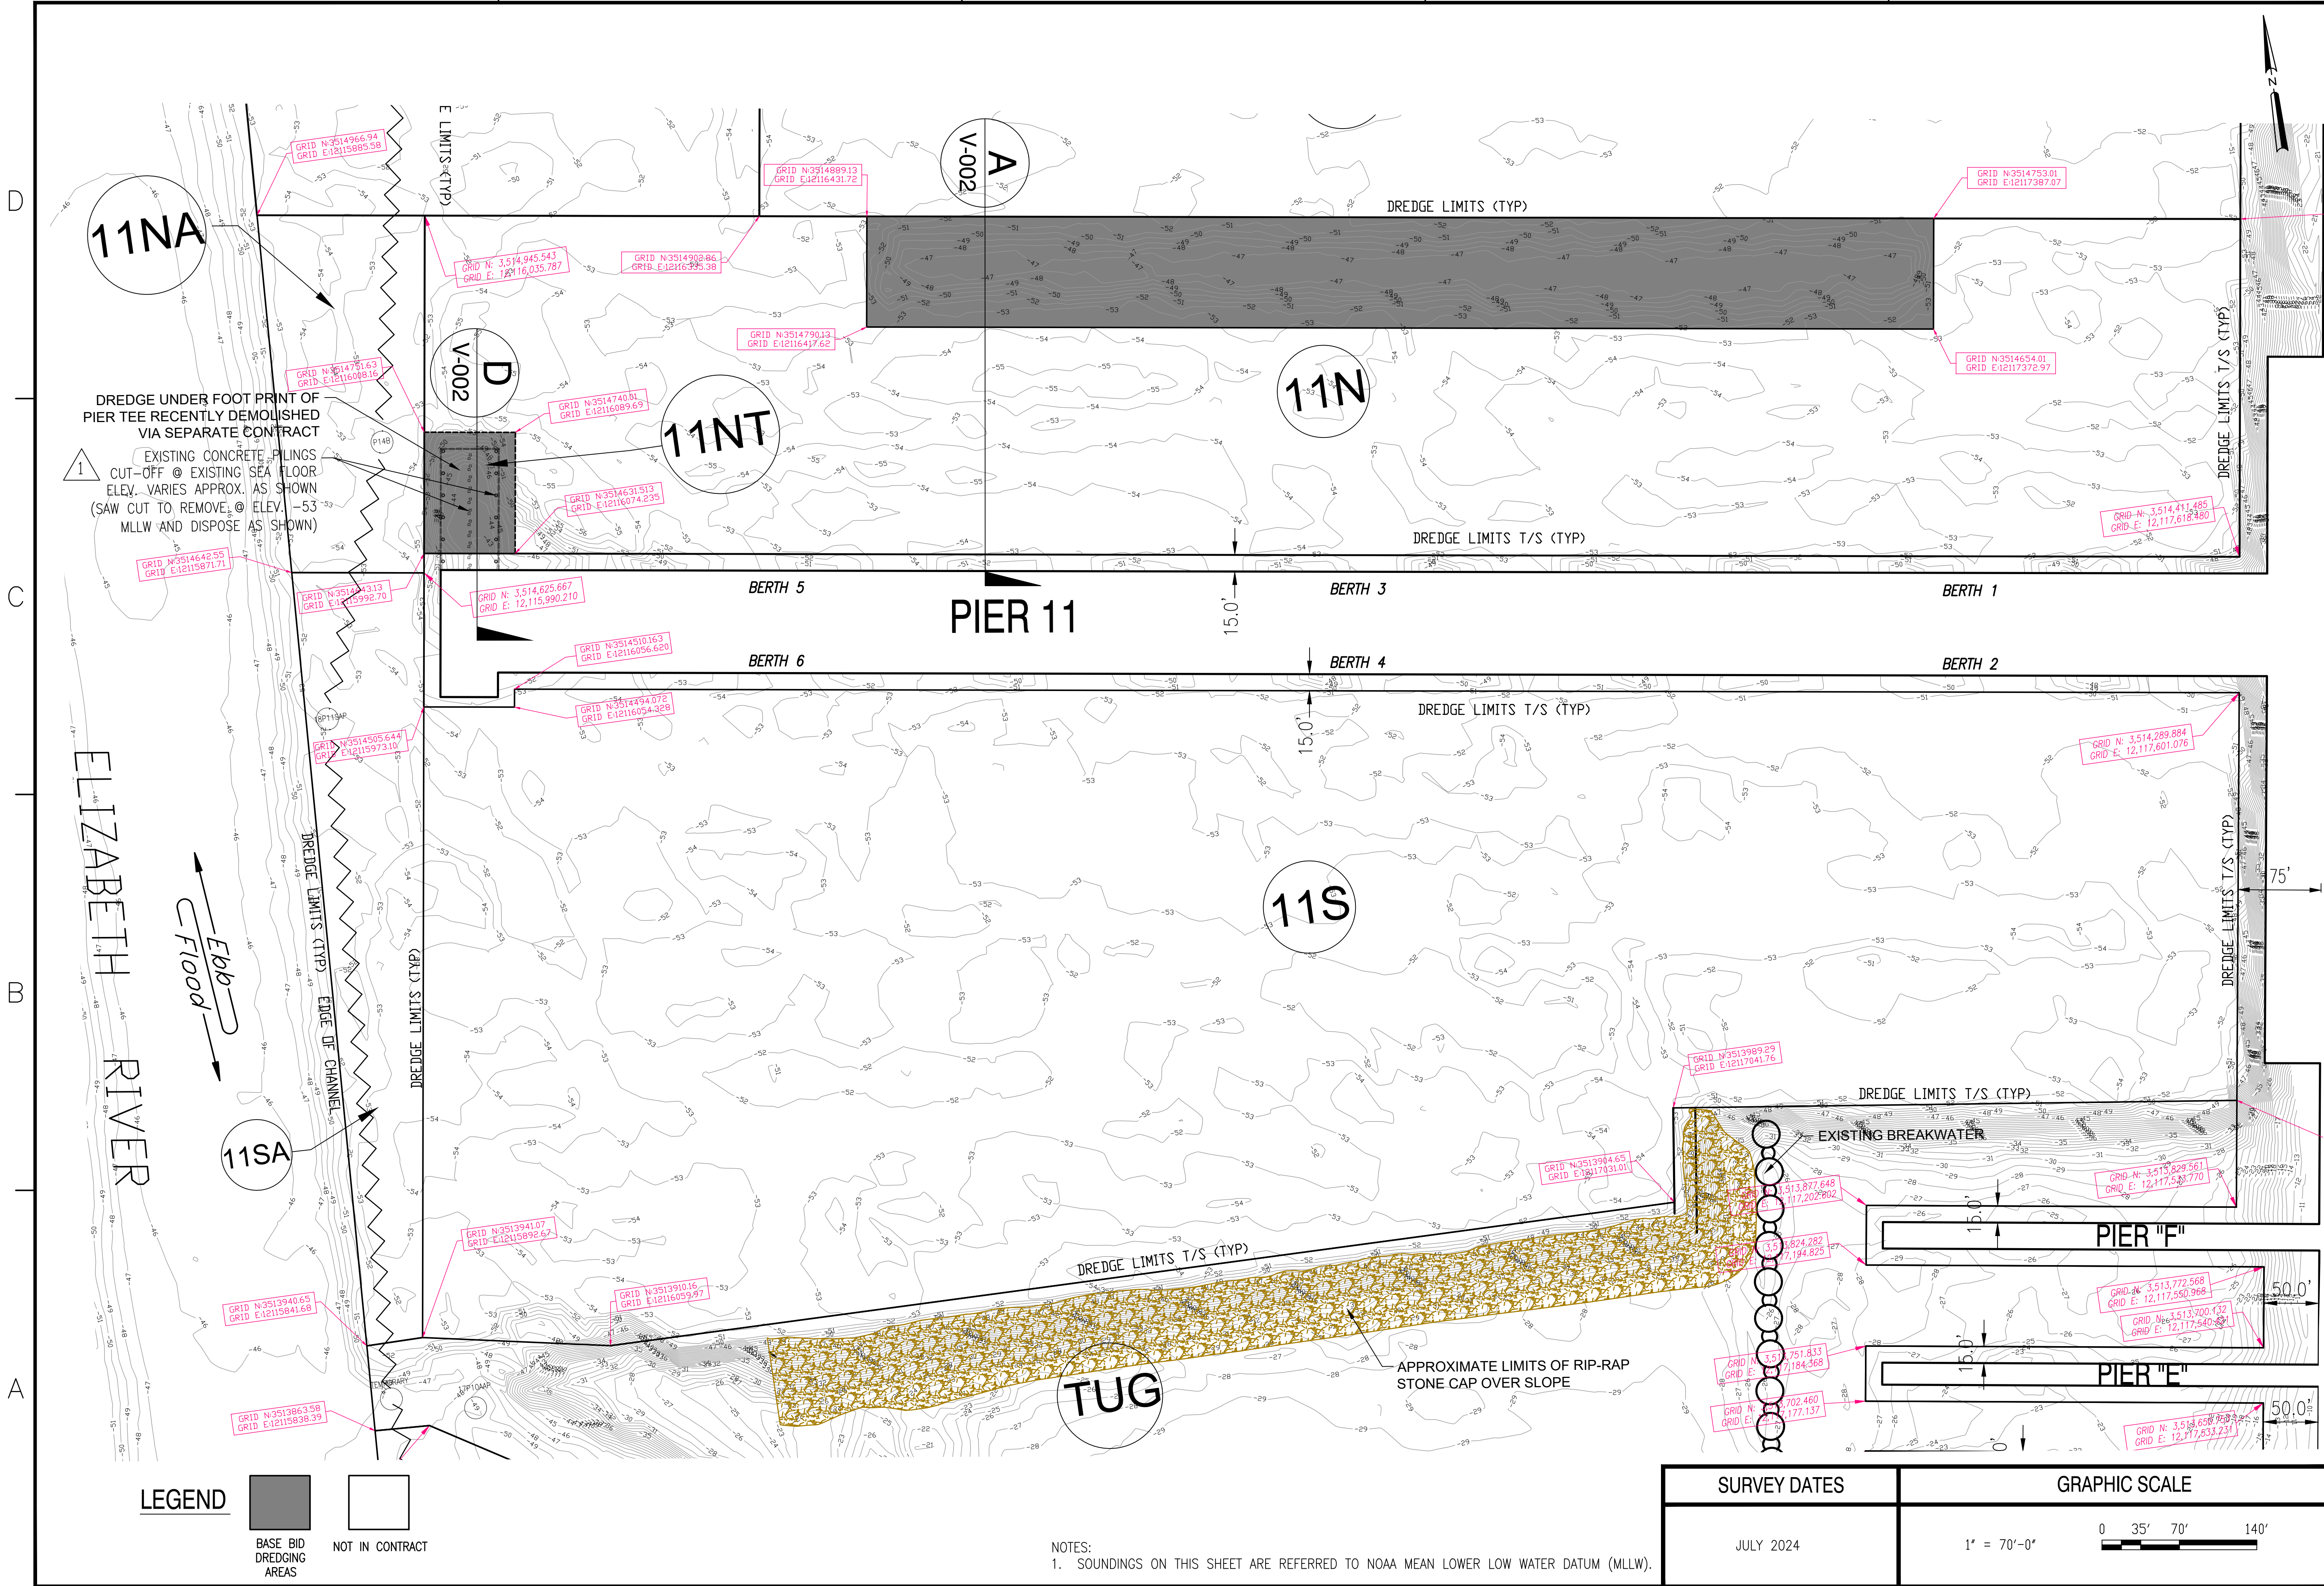

APPROVED BY		DATE	
G-HYDRO BRANCH MGR.		DATE	
APPROVED		DATE	
FOR COMMANDER NAVFAC		DATE	
APPROVED MR. RALPH FILIP		DATE	
NS NORFOLK PORT OPERATIONS		DATE	
PER SAT TO MEMO ON FILE		DATE	
ACTIVITY - SATISFACTORY TO		DATE	
PROJECT MGR. DSG		DATE	
DES: JSG		DATE	
DRW: JSG		DATE	
CHK: JSG		DATE	
FIRE PROTECTION N/A		DATE	
BRANCH MANAGER DLB		DATE	
CHIEF ENG/ARCH EJA		DATE	
NAVAL FACILITIES ENGINEERING SYSTEMS COMMAND		DATE	
NAVAL FACILITIES ENGINEERING COMMAND ~ MID ATLANTIC		DATE	
NAVAL STATION - NORFOLK, VIRGINIA		DATE	
NORFOLK NAVAL STATION		DATE	
NORFOLK, VA		DATE	
SITE PLAN FOR FY 2025 MAINTENANCE DREDGING		DATE	
AT NAVAL STATION NORFOLK		DATE	
PIER 11		DATE	
CODE ID. NO. 80091		DATE	
SCALE: AS NOTED		DATE	
MAXIMO NO.		DATE	
JOB ORDER NO.		DATE	
WORK ORDER NO. 1788443		DATE	
CONSTR. CONTR. NO. N/A		DATE	
NAVFAC DRAWING NO. 12919181		DATE	
SHEET 7 OF 9		DATE	
V-105		DATE	
DRAWING REVISION: 2 FEB 2011		DATE	