


A

B


C

D


| File Name                                                                               | Area              | Date    | Time     | Unit      |
|-----------------------------------------------------------------------------------------|-------------------|---------|----------|-----------|
| \\#District\2-ENG\7.1-Millennium Projects\Santa Fe\CAD\904-FY22-Shrine-00_Santa Fe-Area | Renovation        | 5-18-22 | 04:15:00 | PM        |
|                                                                                         | Areas_Details.dwg |         |          |           |
|                                                                                         |                   |         |          | cemGaussM |

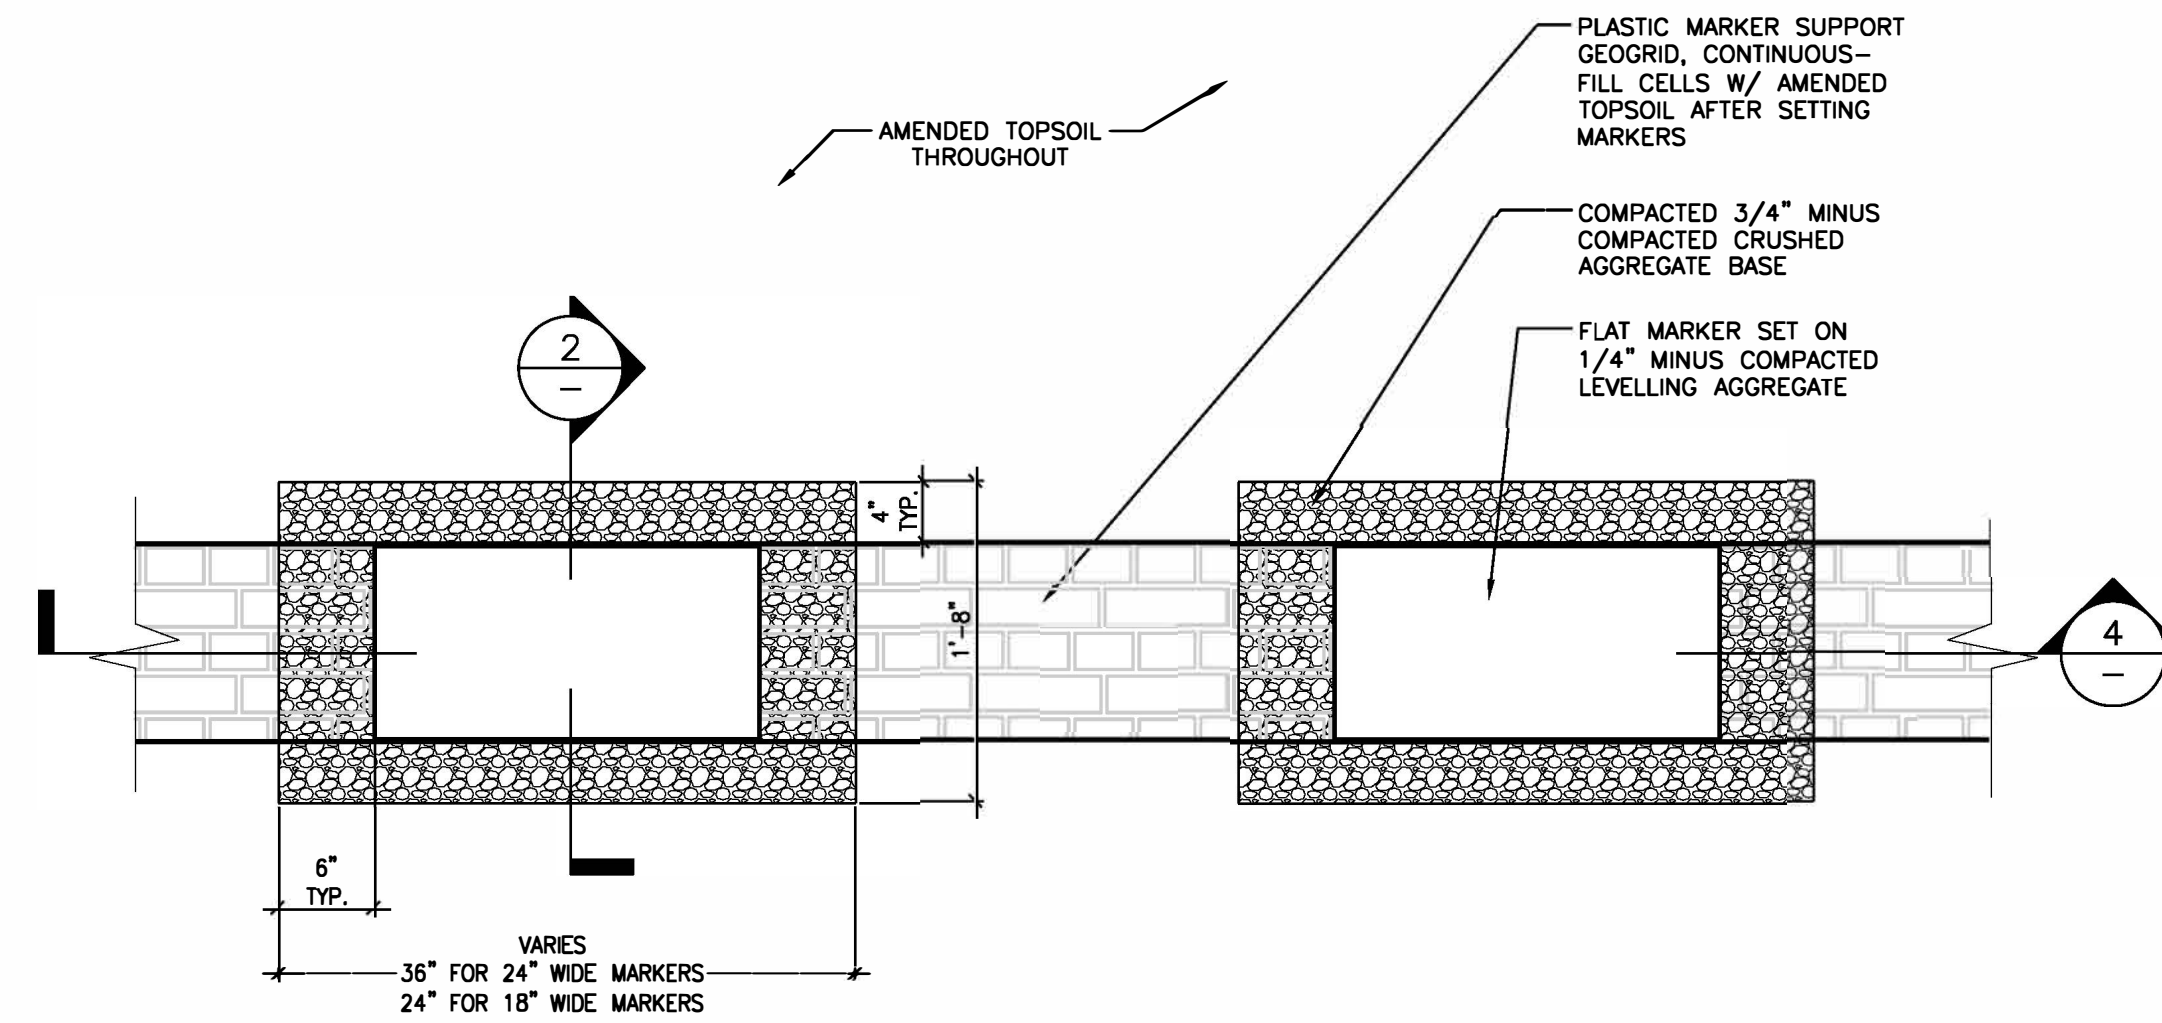


3 FLAT MARKER INSTALLATION (OPTIONS)  
SCALE: N.T.S. PLAN

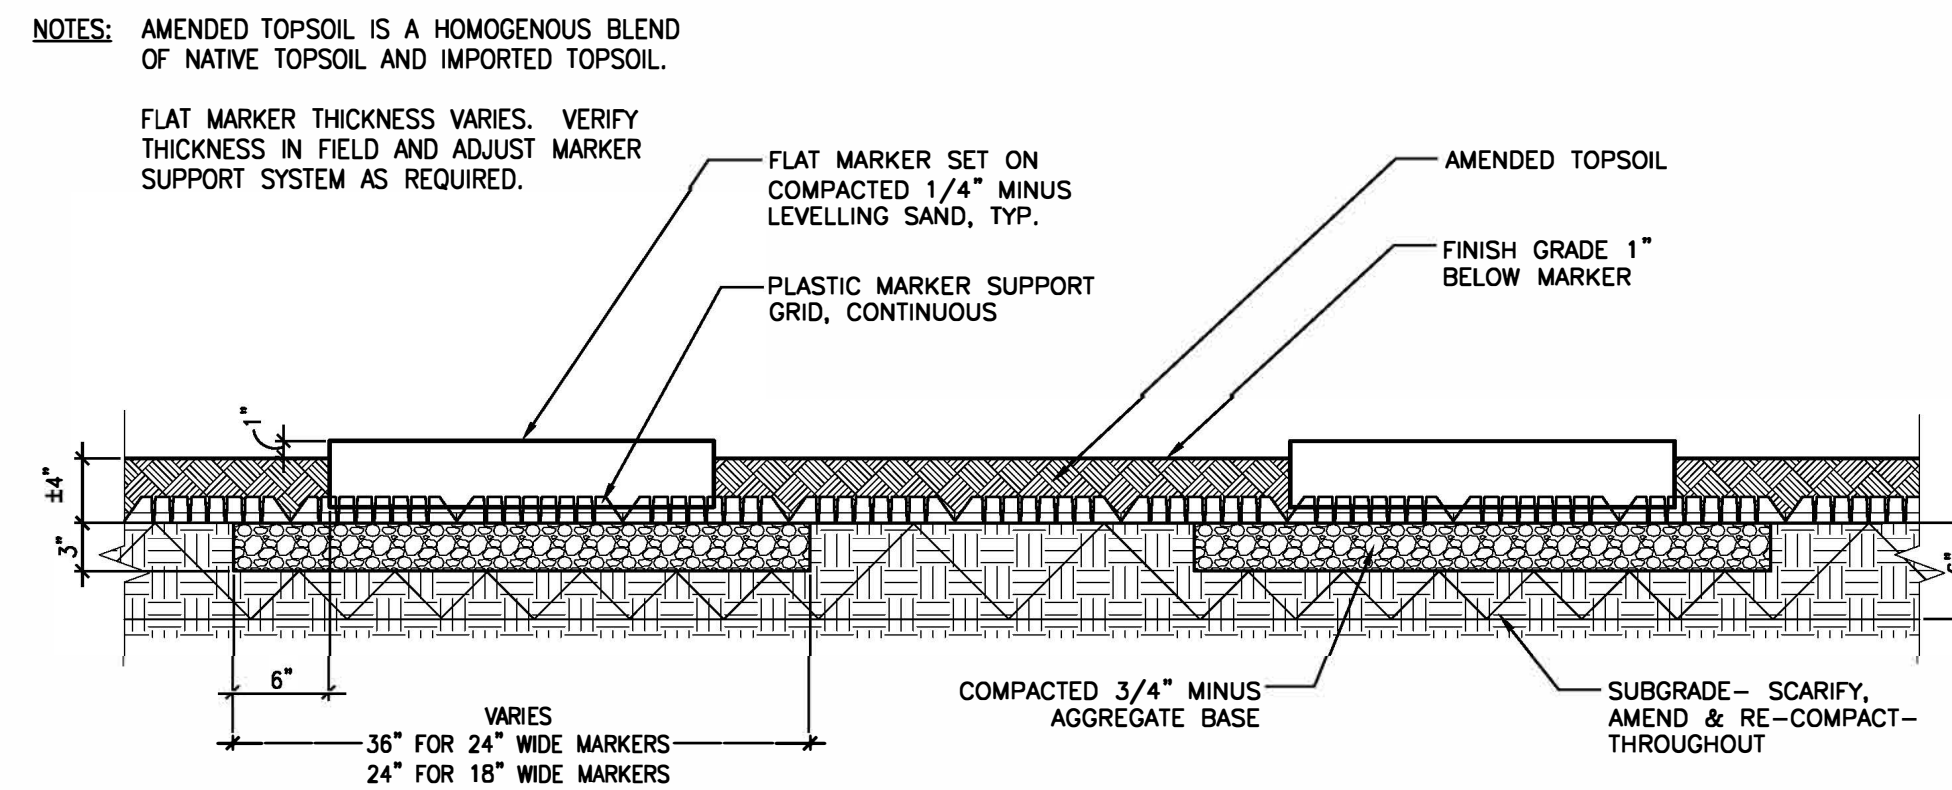

4 FLAT MARKER INSTALLATION (OPTIONS)  
SCALE: N.T.S. SECTION

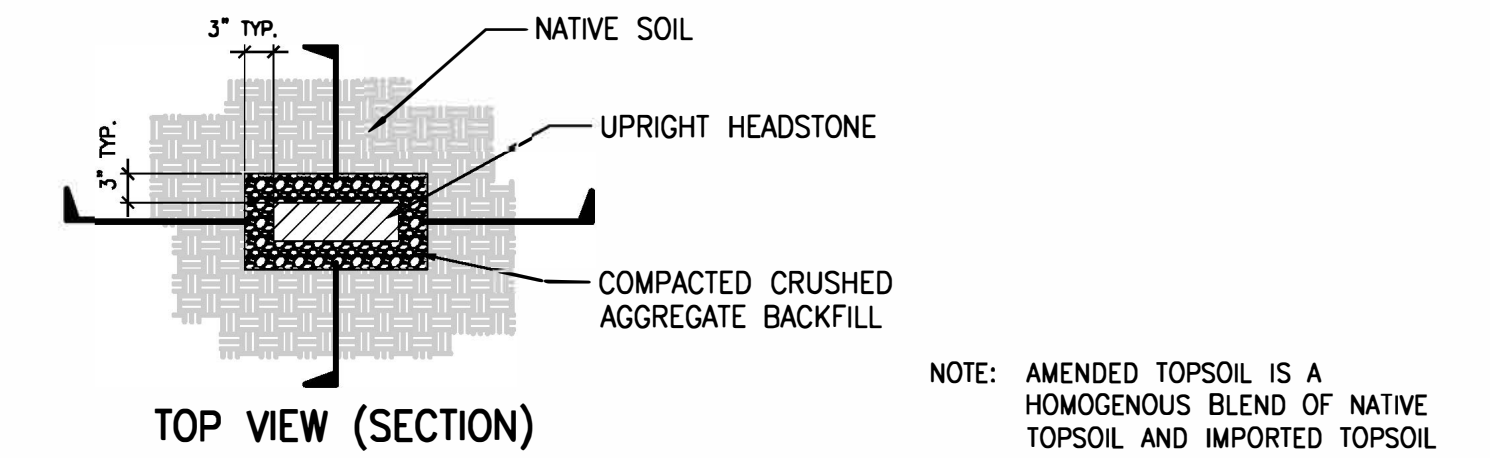


1 UPRIGHT HEADSTONE INSTALLATION (BASE BID)  
SCALE: N.T.S. PLAN/SECTION/CROSS-SECTION

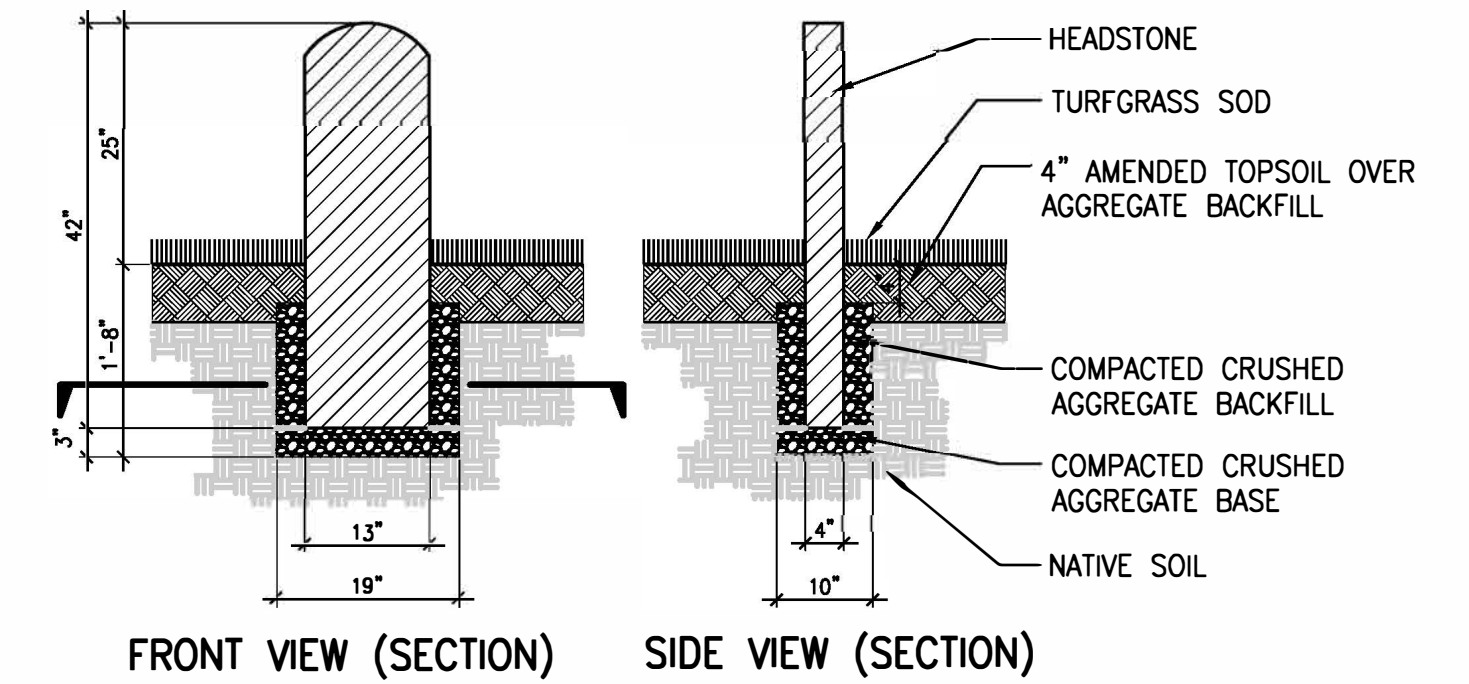

## 2 FLAT MARKER INSTALLATION (OPTIONS)

SCALE: N.T.S. CROSS-SECTION

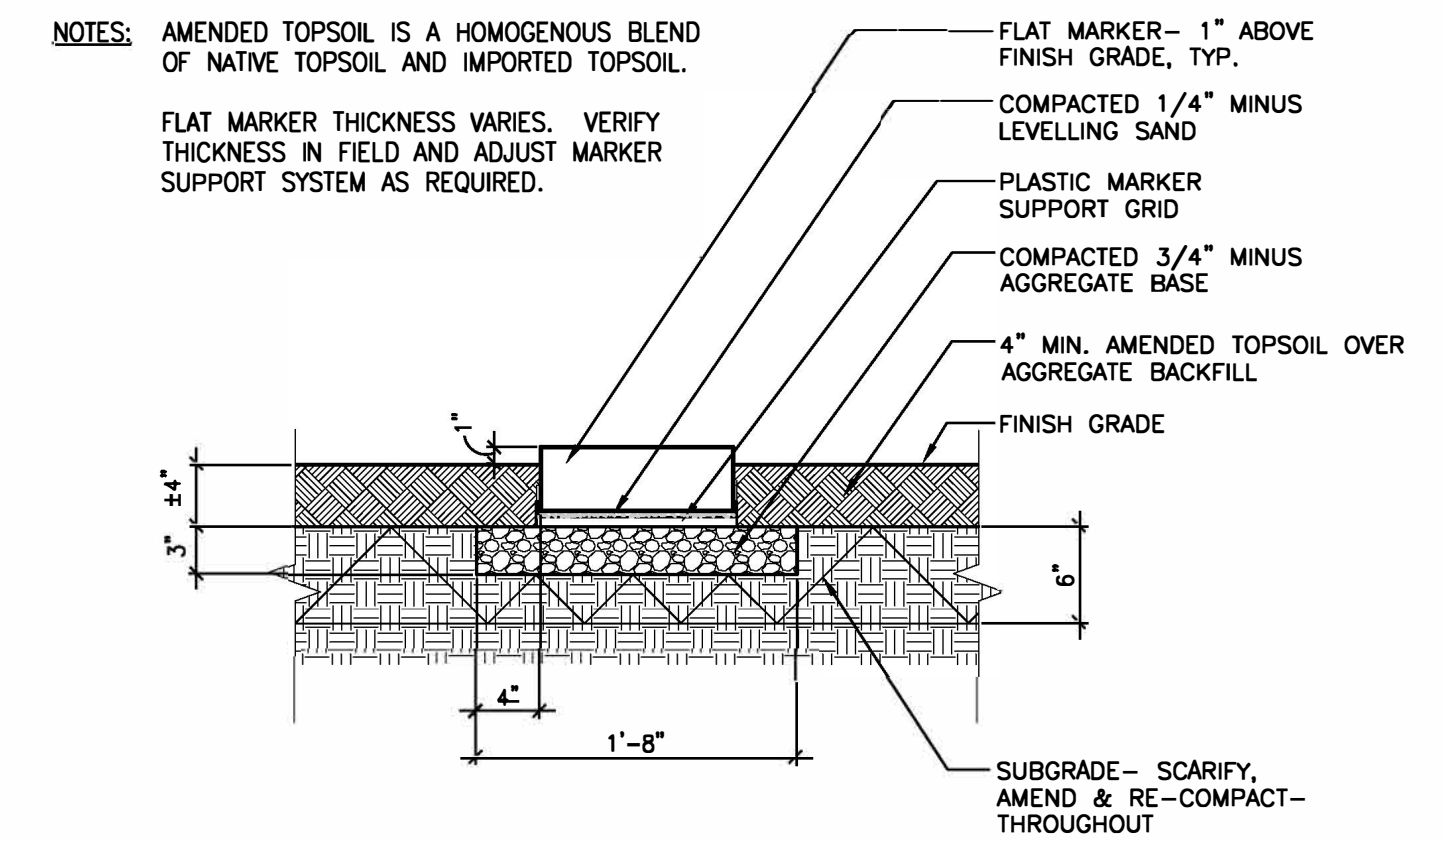

|            |      |   |   |                                                                                   |   |   |
|------------|------|---|---|-----------------------------------------------------------------------------------|---|---|
|            |      |  <div style="display: inline-block; vertical-align: middle; text-align: center;">             NATIONAL<br/>CEMETERY<br/>ADMINISTRATION           </div> | Drawing Title<br><div style="text-align: center; font-weight: bold;">EXHIBIT 'B'</div> <div style="text-align: center; font-weight: bold;">HEADSTONE SETTING DETAILS</div> | Project Title<br><div style="height: 40px; border: 1px solid black;"></div>       | Project Number<br><div style="height: 40px; border: 1px solid black;"></div>                                                                       | <div style="text-align: center; font-weight: bold;">National Cemetery Administration</div> <div style="text-align: center;">              Department of Veterans Affairs           </div> |
|            |      |   | Approved Project Director<br><div style="height: 40px; border: 1px solid black;"></div>                                                                                    | Location<br>Santa Fe National Cemetery<br>501 Guadalupe St.<br>Santa Fe, NM 87501 | Drawing Number<br><div style="font-size: 2em; font-weight: bold; text-align: center;">L-2</div> <div style="text-align: center;">Dwg. 2 of 2</div> |   |
|            |      |   |   | Date<br><div style="height: 40px; border: 1px solid black;"></div>                |   |   |
|            |      |   |   |                                                                                   |   |   |
|            |      |   |   |                                                                                   |   |   |
|            |      |   |   |                                                                                   |   |   |
| Revisions: | Date |   |   |                                                                                   |   |   |