



KITCHEN RENOVATION PROJECT

PROJET DE RENOVATION DE CUISINE

MAITRE D'OUVRAGE / OWNER: US CONSUL GENERAL OF CASABLANCA

REVISIONS:	9 OCT 2024	OWNER REVIEW
	23 DEC 2025	PLAN CHECK 1
	6 JAN 2026	PLAN CHECK 2
	2 FEB 2026	FOR BID

INDEX:

ARCHITECTURAL PLANS

1. COVER SHEET
2. PROJECT LOCATION AND GENERAL NOTES
3. DEMOLITION FLOOR PLAN
4. DEMOLITION CEILING PLAN
5. FINISH SCHEDULE
6. EQUIPMENT SCHEDULE
7. CONSTRUCTION PLAN
8. EQUIPMENT PLAN
9. FINISH PLAN
- 10.ELEVATION
- 11.ELEVATION
- 12.ELEVATION
- 13.ELEVATION
- 14.CEILING PLAN
- 15.LIGHTING PLAN
- 16.MILLWORK PLAN
- 17.DOOR DETAIL
- 18.MILLWORK DETAIL
- 19.MILLWORK DETAIL
- 20.MILLWORK DETAIL
- 21.MILLWORK DETAIL
- 22.MILLWORK DETAIL
- 23.MILLWORK DETAIL
- 24.MILLWORK DETAIL
- 25.MILLWORK DETAIL
- 26.MILLWORK DETAIL
- 27.MILLWORK DETAIL
- 28.MILLWORK DETAIL
- 29.MILLWORK DETAIL

ENGINEERING PLANS

- PLUMBING PLANS - SUPPLY
- PLUMBING PLANS - SANITARY
- MECHANICAL PLAN
- ELECTRICAL LIGHTING PLAN
- ELECTRICAL POWER PLAN

SPECIFICATIONS

- PROTECTIONS OF EXISTING CONDITIONS
- ELECTRICAL
- PLUMBING


PROJECT LOCATION AND GENERAL NOTES

1. This property is a cultural heritage resource owned and operated by the USG and as such all work shall be in compliance with the Secretary of Interior Standards for Historic Preservation.
2. The Contractor perform a pre-construction damage report of all character defining elements of the heritage property to include all cracks, spalls, holes, stains, etc. USG shall review conditions and agree of extents. All conditions which are new or existing conditions made worse will be required to be repaired by the contractor using conservation principles and methods at no expense to the owner. OBO CH shall review and approve all means, methods and materials for architectural repairs.

3. Contractor shall limit vibrations to minimize potential disturbance to sensitive, brittle and irreplaceable architectural finishes throughout the residence.
4. Contractor ia responsible to protect and or remove existing heritage collections in the areas surrounding the kitchen, to include furniture, paintings, fine art, rugs, pianos, books, etc. Please coordinate with OBO Office of Cultural Heritage for listing of heritage objects and requirements for protection, assessment and cataloguing.
5. No penetrations in structural members are permitted. If a penetration is determined to be required, architect and owner must be notified to coordinate approach prior to performing the work.



site plan
situation sur maps

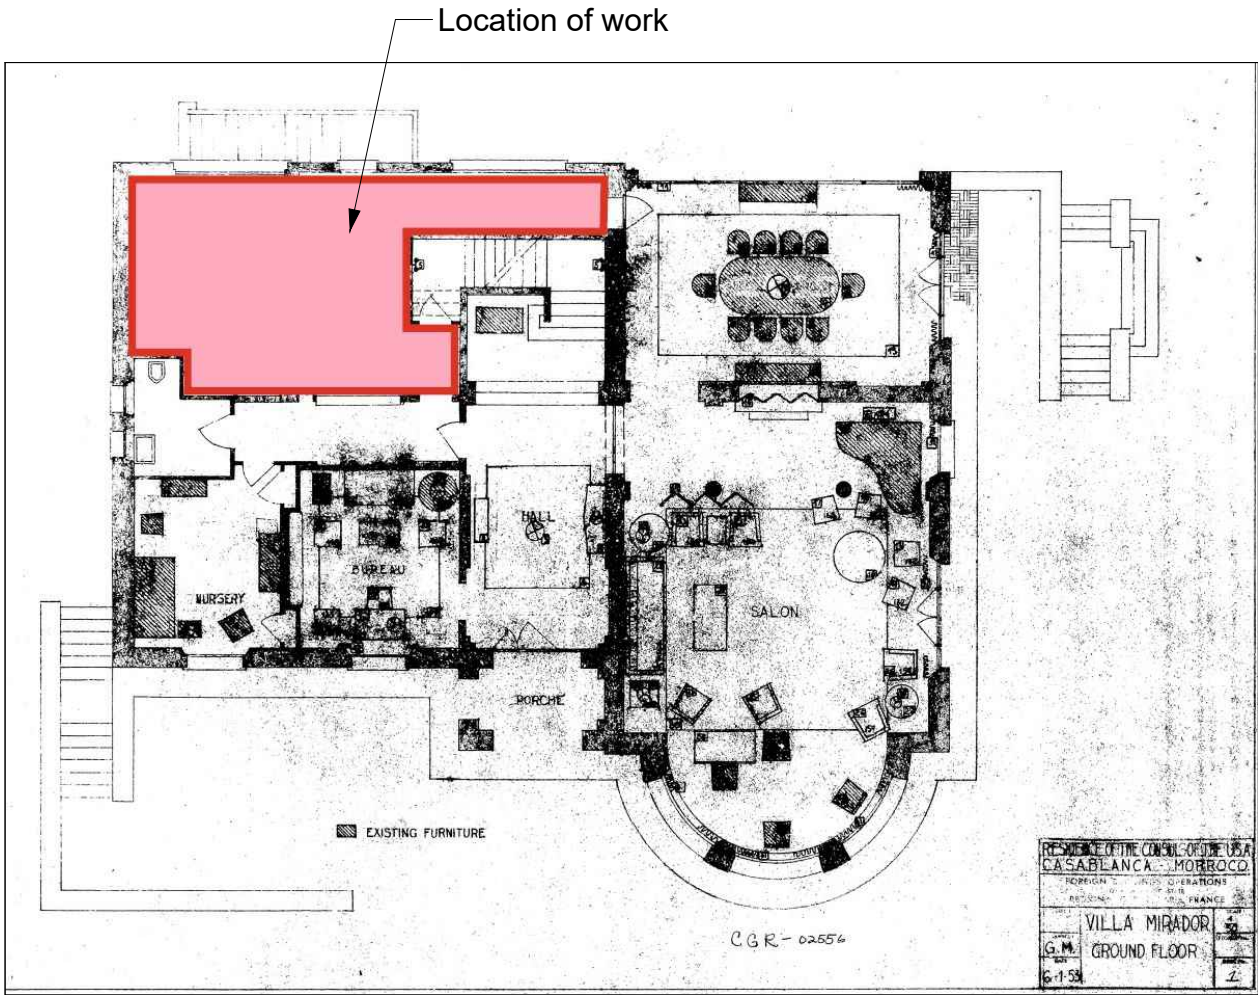


location in villa
situation sur maison


CONTRACTOR NOTES:

- 1. Protect existing construction to remain
- 2. Dispose of removed items off site in a legal manner.
- 3. Prevent dust and debris from escaping area of work.
- 4. See electrical and mechanical plans for other items to demolish

REMARQUES À L'ENTREPRENEUR :

- 1. Protéger la construction existante pour qu'elle reste en place
- 2. Éliminer les éléments retirés hors du site de manière légale.
- 3. Empêcher la poussière et les débris de s'échapper de la zone de travail.
- 4. Voir les plans électriques et mécaniques pour les autres éléments à démolir

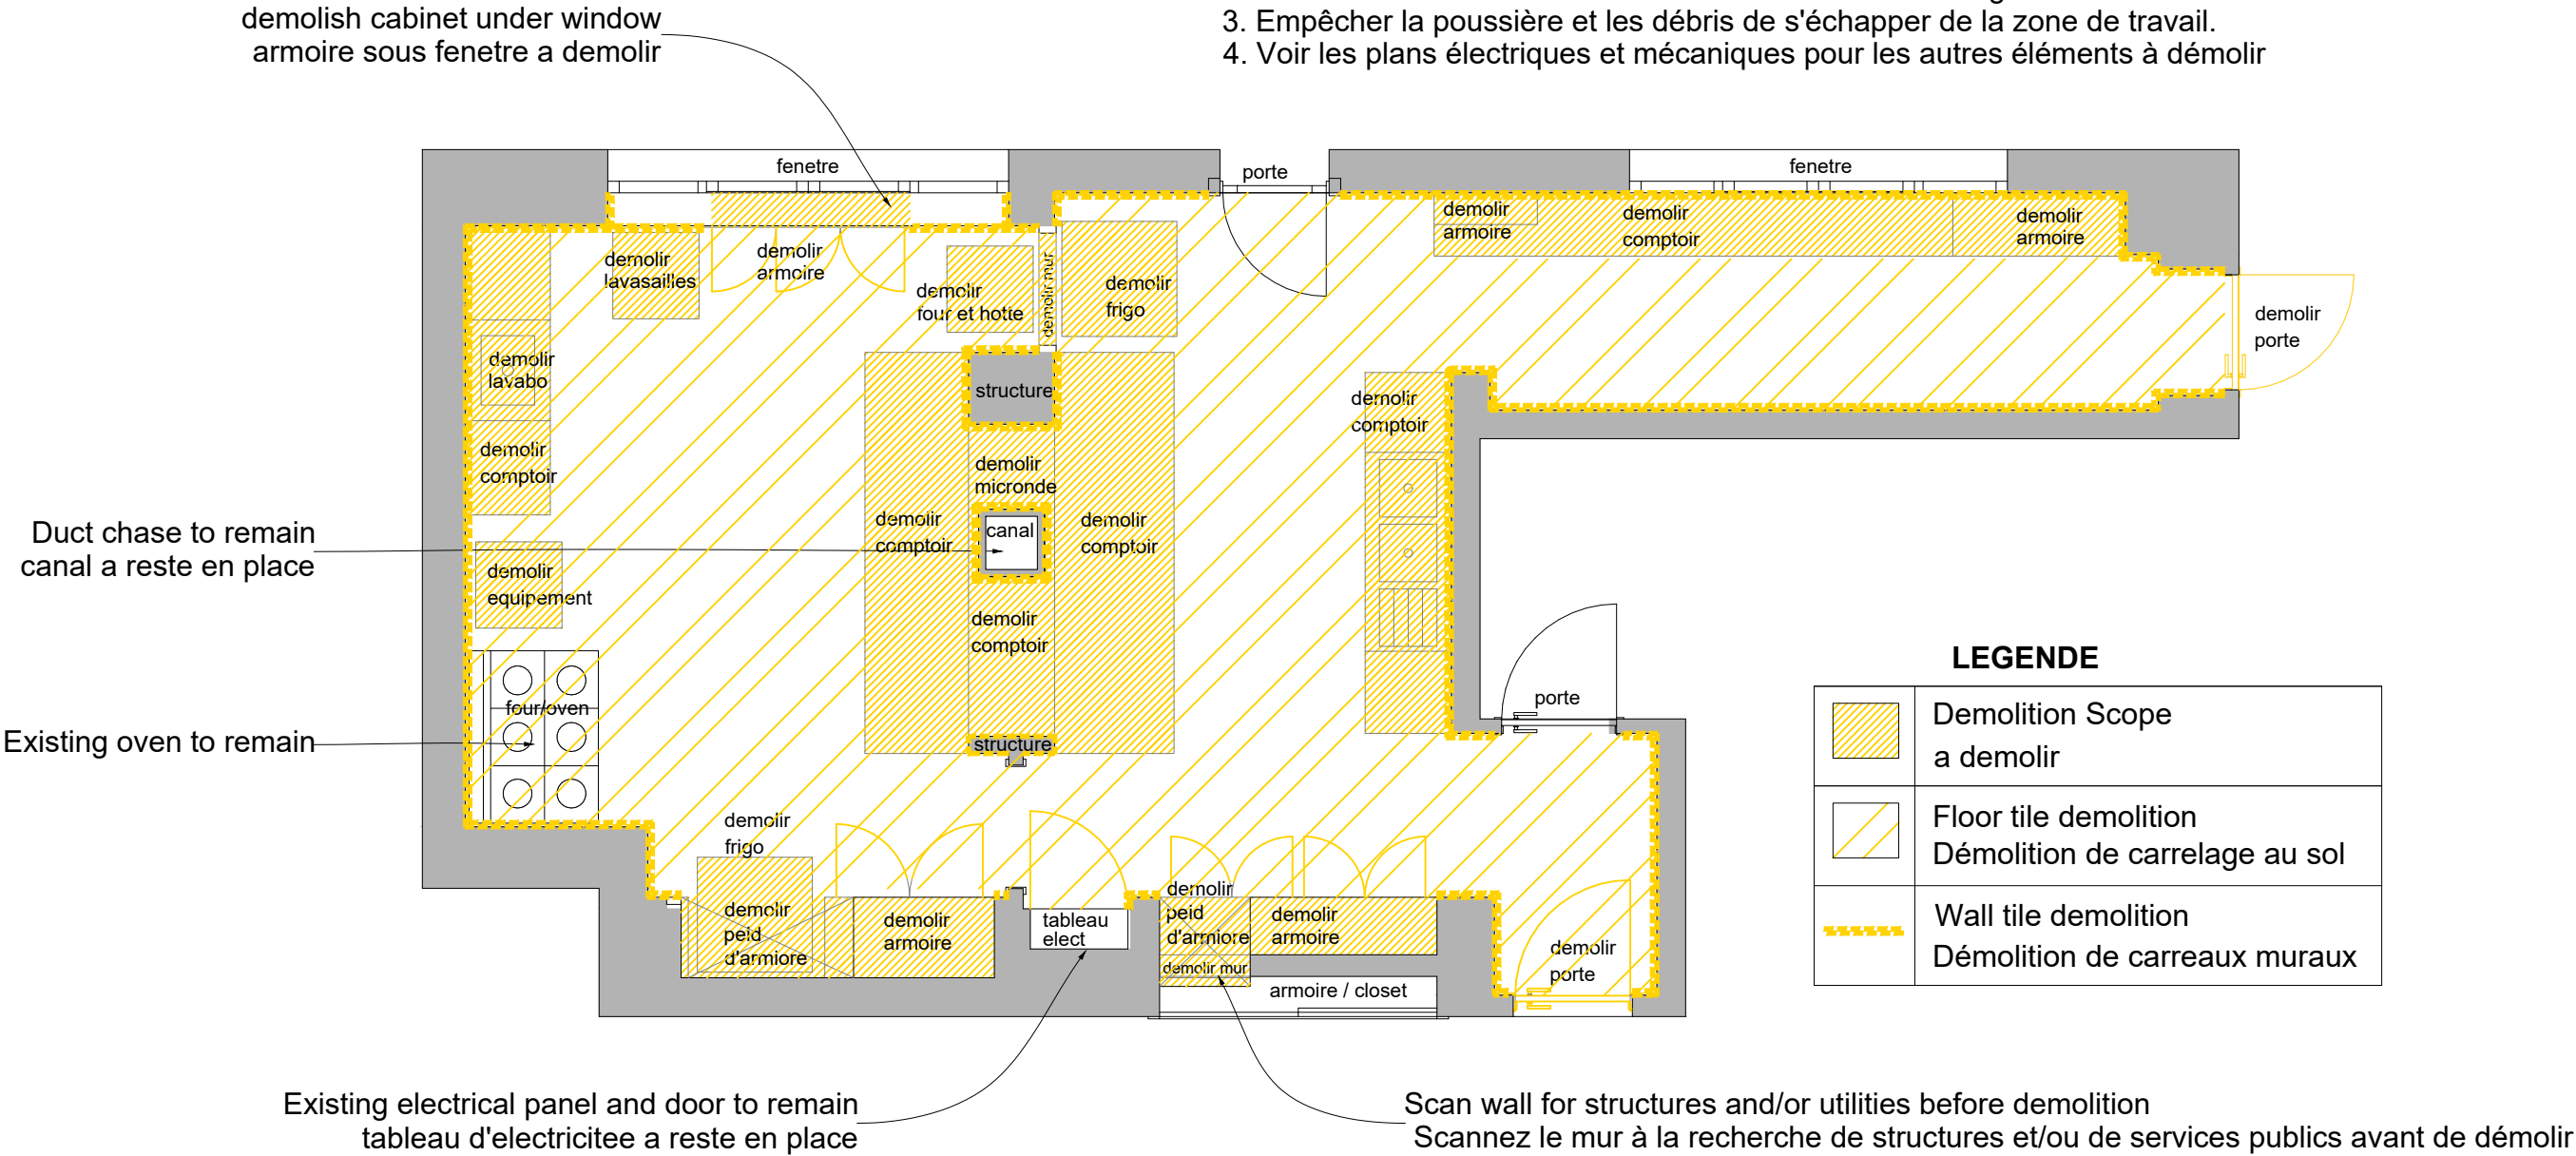

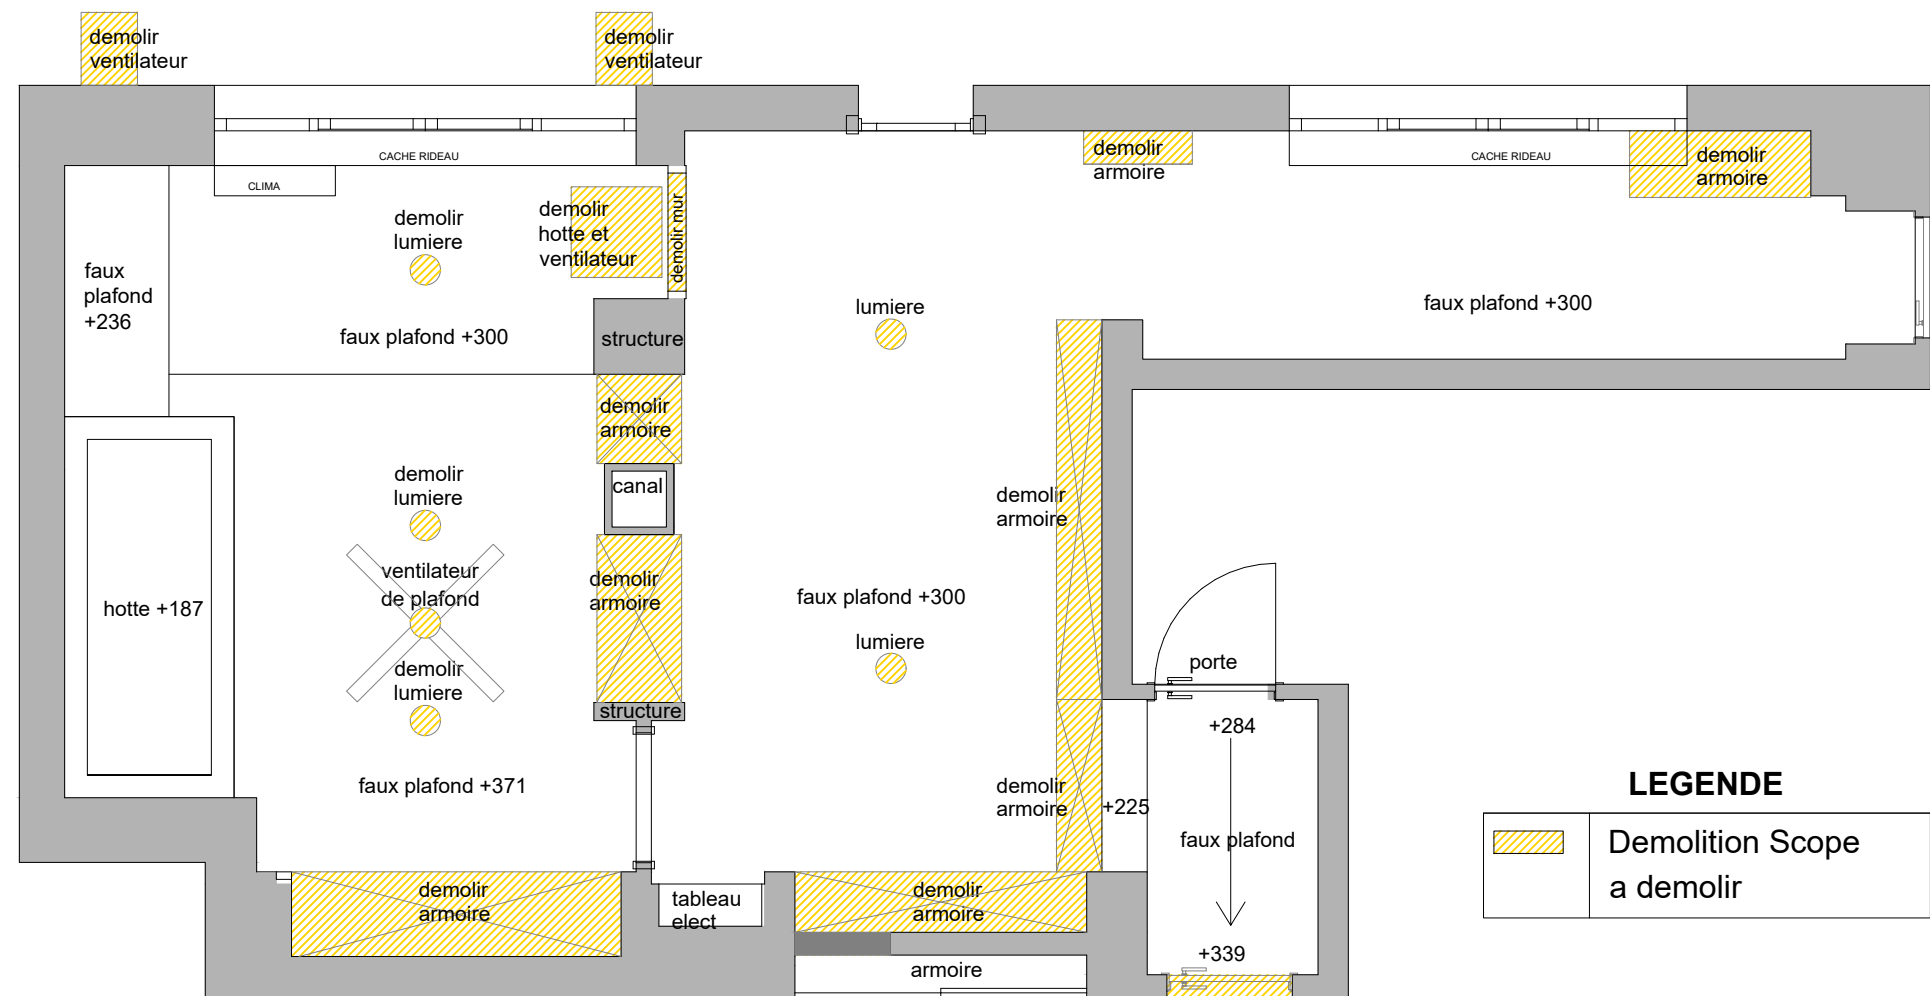

Tag	Description	Manufacturer	Model/color	Contact	Qty	Unit	Unit Price (MAD)	Price
T1	Floor tile	Popham Design	Square 20 x 20 x 1,2 cm with HYDROFUGE sealant Black/white, Custom mold	Tassoultante - Marrakech T: +212.524.378.022 chaimaa@pophamdesign.com	45	m2	608	27,360
	Grout							
Q	Countertops - Quartz ALT Imitation white Carrera marble	Cupastone Ceratop https://www.ceratop.ma/	Borghini	Horizon Marbre Km 17 Avenue Hassan II Quartier Industriel, TEMARA contact@horizonmarbre.ma tel:+212537643009 Othame - see card +212 0666864145 othmane21.horizon@gmail.com	12.5	m2	1,900	23,750
T2	Wall base	Argena	Serie TANUM Color: BLACK Large format 30x90 cm tile Field cut 10cm strips	Sara Cerame Temara Sadikh Diouf +212 666 80 82 01 sadikh@saracerame.com	4.6	m2	195	897
T3	Wall Tile "Subway Tile"	Dune Piccalo	METRO Rectangular 10 x 20 cm White GLOSSY Beveled edges Horizontal 25% running bond Light gray grout joints 0.5 mm	Sara Cerame	32.0	m2	350	11,200
	Grout - both floor tile and wall tile	Weber Saint Gobain	Junta Fina Porcelanica Light gray	Conquete or Sara Cerame				
	Tile termination edges and outside corners	Schluter	QUADEC	MISHIMA INDUSTRIES Contact: Issam El Mouthadi Résidence du Palais Boulevard Ghandi n°19 20 000 CASABLANCA Tél: (+212) 661 61 95 11 issam@mishimaindustries.com	17.0	m		
T4	Zelige	Art Naji	Traditional Zelige ELABORATE black/white/gray Price includes installation @ 250 dh/m2	Art Naji 20, Quartier Industriel Ain Nokbi 30120 Fez info@artnaji.com +212 535 66 91 66 Othmane +212 661-932426	2.5	m2	2,750	6,875
P1	Paint - white ceiling	Colorado Paint-All	S 0500-N	Colorado	65.0	m2		
P1	Paint - white walls	Colorado Paint-All	S 0500-N	Colorado	45.0	m2		
P2	Paint - light gray walls	Colorado Paint-All	S 1000-N or S 2000-N	Colorado	35.0	m2		
P2	Wood Cabinets Solid wood and Plywood Paint - light gray	Colorado Paint-All	S 1000-N or S 2000-N	Conquete	See plans			
P3	Paint - dark gray Wood doors and frames	Colorado Paint-All	S 8000-N	Colorado	See plans			
P3M	Metal Cabinets Metal doors and frames Paint - dark gray	Colorado Metalac	S 8000-N	Colorado	See plans			
P3M	Paint - dark gray Metal Upper cabinets	Colorado Metalac	S 8000-N	Colorado 5, Allee des Orchidees Ain Sebaa - Casablanca +212 522 35 23 35	See plans			
C1	Cabinet pulls (poignées)	Ikea	BAGGANÄS Black 143 mm	IKEA Zenata +212 520-100900	See plans			
G1	Fluted glass	Tolba Verre? (recommended by Othmane @ Horizon	Clear, tempered 3mm thick 3mm fluting	N/A	6	m2		
	Frost film - optional				6	m2		

CONTRACTOR NOTES:

1. Quantities are for estimation purposes only and does not include overrun. Contractor is repsonsible for providing necessary quantities based on drawings.

2 Provide silicone sealant at all inside corners, color to match adjacent finish.

3. Contractor to submit two samples (to architect and owner) for review and approval before purchase and installation

4. All surfaces are to be prepared and cleaned per manufactucturer recommendations before installation of finishes.

REMARQUES À L'ENTREPRENEUR :

1. Les quantités sont fournies à titre d'estimation uniquement et n'incluent pas les dépassements. L'entrepreneur est responsable de fournir les quantités nécessaires en fonction des dessins.

2. Fournir un mastic silicone dans tous les coins intérieurs, de couleur assortie à la finition adjacente.


3. L'entrepreneur doit soumettre deux échantillons (à l'architecte et au propriétaire) pour examen et approbation avant l'achat et l'installation.

4. Toutes les surfaces doivent être préparées et nettoyées conformément aux recommandations du fabricant avant l'installation des finitions.

Description	Manufacturer	Model/color	Contact	Qty	Unit Price (mad)	Total	Comments
APPLICANCES							
Four-door fridge with convertible freezer zones AND water filling station 585L Hauteur (cm) 179 Largeur (cm) 91 Profondeur (cm) 75	AEG	AQE6879BA	Electroplanet	2	30,000	60,000	
Four-door fridge with convertible freezer zones 591L Hauteur (cm) 187,5 Largeur (cm) 90,9 Profondeur (cm) 70.1	Whirlpool	WQ9 B1L/U1L	Electroplanet		24,000		Alternate
Four-door fridge with convertible freezer zones 655L Hauteur (cm) 179 Largeur (cm) 91.3 Profondeur (cm) 73,5	LG	LG GR-B257SLWL	Electroplanet		20,500		Alternate
Plaque cuisine Four-burner gas range (60x60cm)	Whirlpool	PMW75D2 IXELIUM	Electroplanet	1	5,300	5,300	
	Franke	TC FHC604 NOIR	Electroplanet		6,290		Alternate
	Bosch	PCP6A5B90	Electroplanet		3,900		Alternate
Salamander warming oven (75x35x45cm)	GMG	SLM60	Cuisine Pro Maroc	1	4,000	4,000	
Micro-onde encasrtable Built-in Microwave (60x40x40cm)	Whirlpool	AMW836IXL	Electroplanet	1	6,120	6,120	
	Bosch	BFL524MB0	Electroplanet		4,500		Alternate
	AEG	MBB1756DEM	Electroplanet		4,500		Alternate
Four Encastrable Built-in electric Oven (60x60x60cm)	Whirlpool	W9 OM24S1H	Electroplanet	1	7,700	7,700	
	AEG	BSK792220M	Electroplanet		13,000		Alternate
	Franke	FMA 97 P XS 60CM	Electroplanet		8,000		Alternate
Lavevasaille Dishwasher (60x60x85cm)	Whirlpool	W7F HS41 X	Electroplanet	1	8,500	8,500	
	Bosch	SMS8YDI82T	Electroplanet		13,000		Alternate
	AEG	FFB83836PM FFB93807PM	Electroplanet		10,000		Alternate
PLUMBING							
Evier Two-bowel sink (40x34x17.5cm) under mount sink with drain board cut into coutnertop	Blanco	ANDANO 340/340-U stainless	Conquete	2	3,600	7,200	
MITIGEUR Faucet with flexible hose	Blanco	CATRIS-S 521476 chrome	Conquete	1		0	
MITIGEUR Faucet, standard	Blanco	MIDA 517742 chrome	Conquete	1		0	
Pot filler faucet over small range	Kohler	K-35745 chrome	Conquete	1		0	
Floor Drain (optional)	ACO	Netsol ACO 401124	Conquete	2		0	
LIGHTING							
Plafonnier "A" Large round ceiling lights in main space	EGLO	900067 MARGHERA-Z	EGLO	4	4,489	17,956	
Plafonnier "B" Small round ceiling light in vestibule	EGLO	99215 FUEVA 5	EGLO	1	119	119	
Applique "C" Accent light over Zellige	Brilliant	INHK20728S22	Luxalight	1	119	119	
Plafonnier Spot "D" Surface mounted spots	Brilliant	Bogus Round INHK19813S05	Luxalight	9	128	1,152	
Chemin LED "E" LED tape under cabinets		ENGINEER SPEC		8m			
Ceiling Fan "F" Ventilateur de plafond	Faro	PUNT TUB M BLANC REF 33828 white					

CONTRACTOR NOTES:
Contractor to confirm all quantities before ordering and installing

REMARQUES À
L'ENTREPRENEUR :
Le Constructeur doit confirmer toutes les sélections d'équipement avec le propriétaire et l'architecte avant de commander.

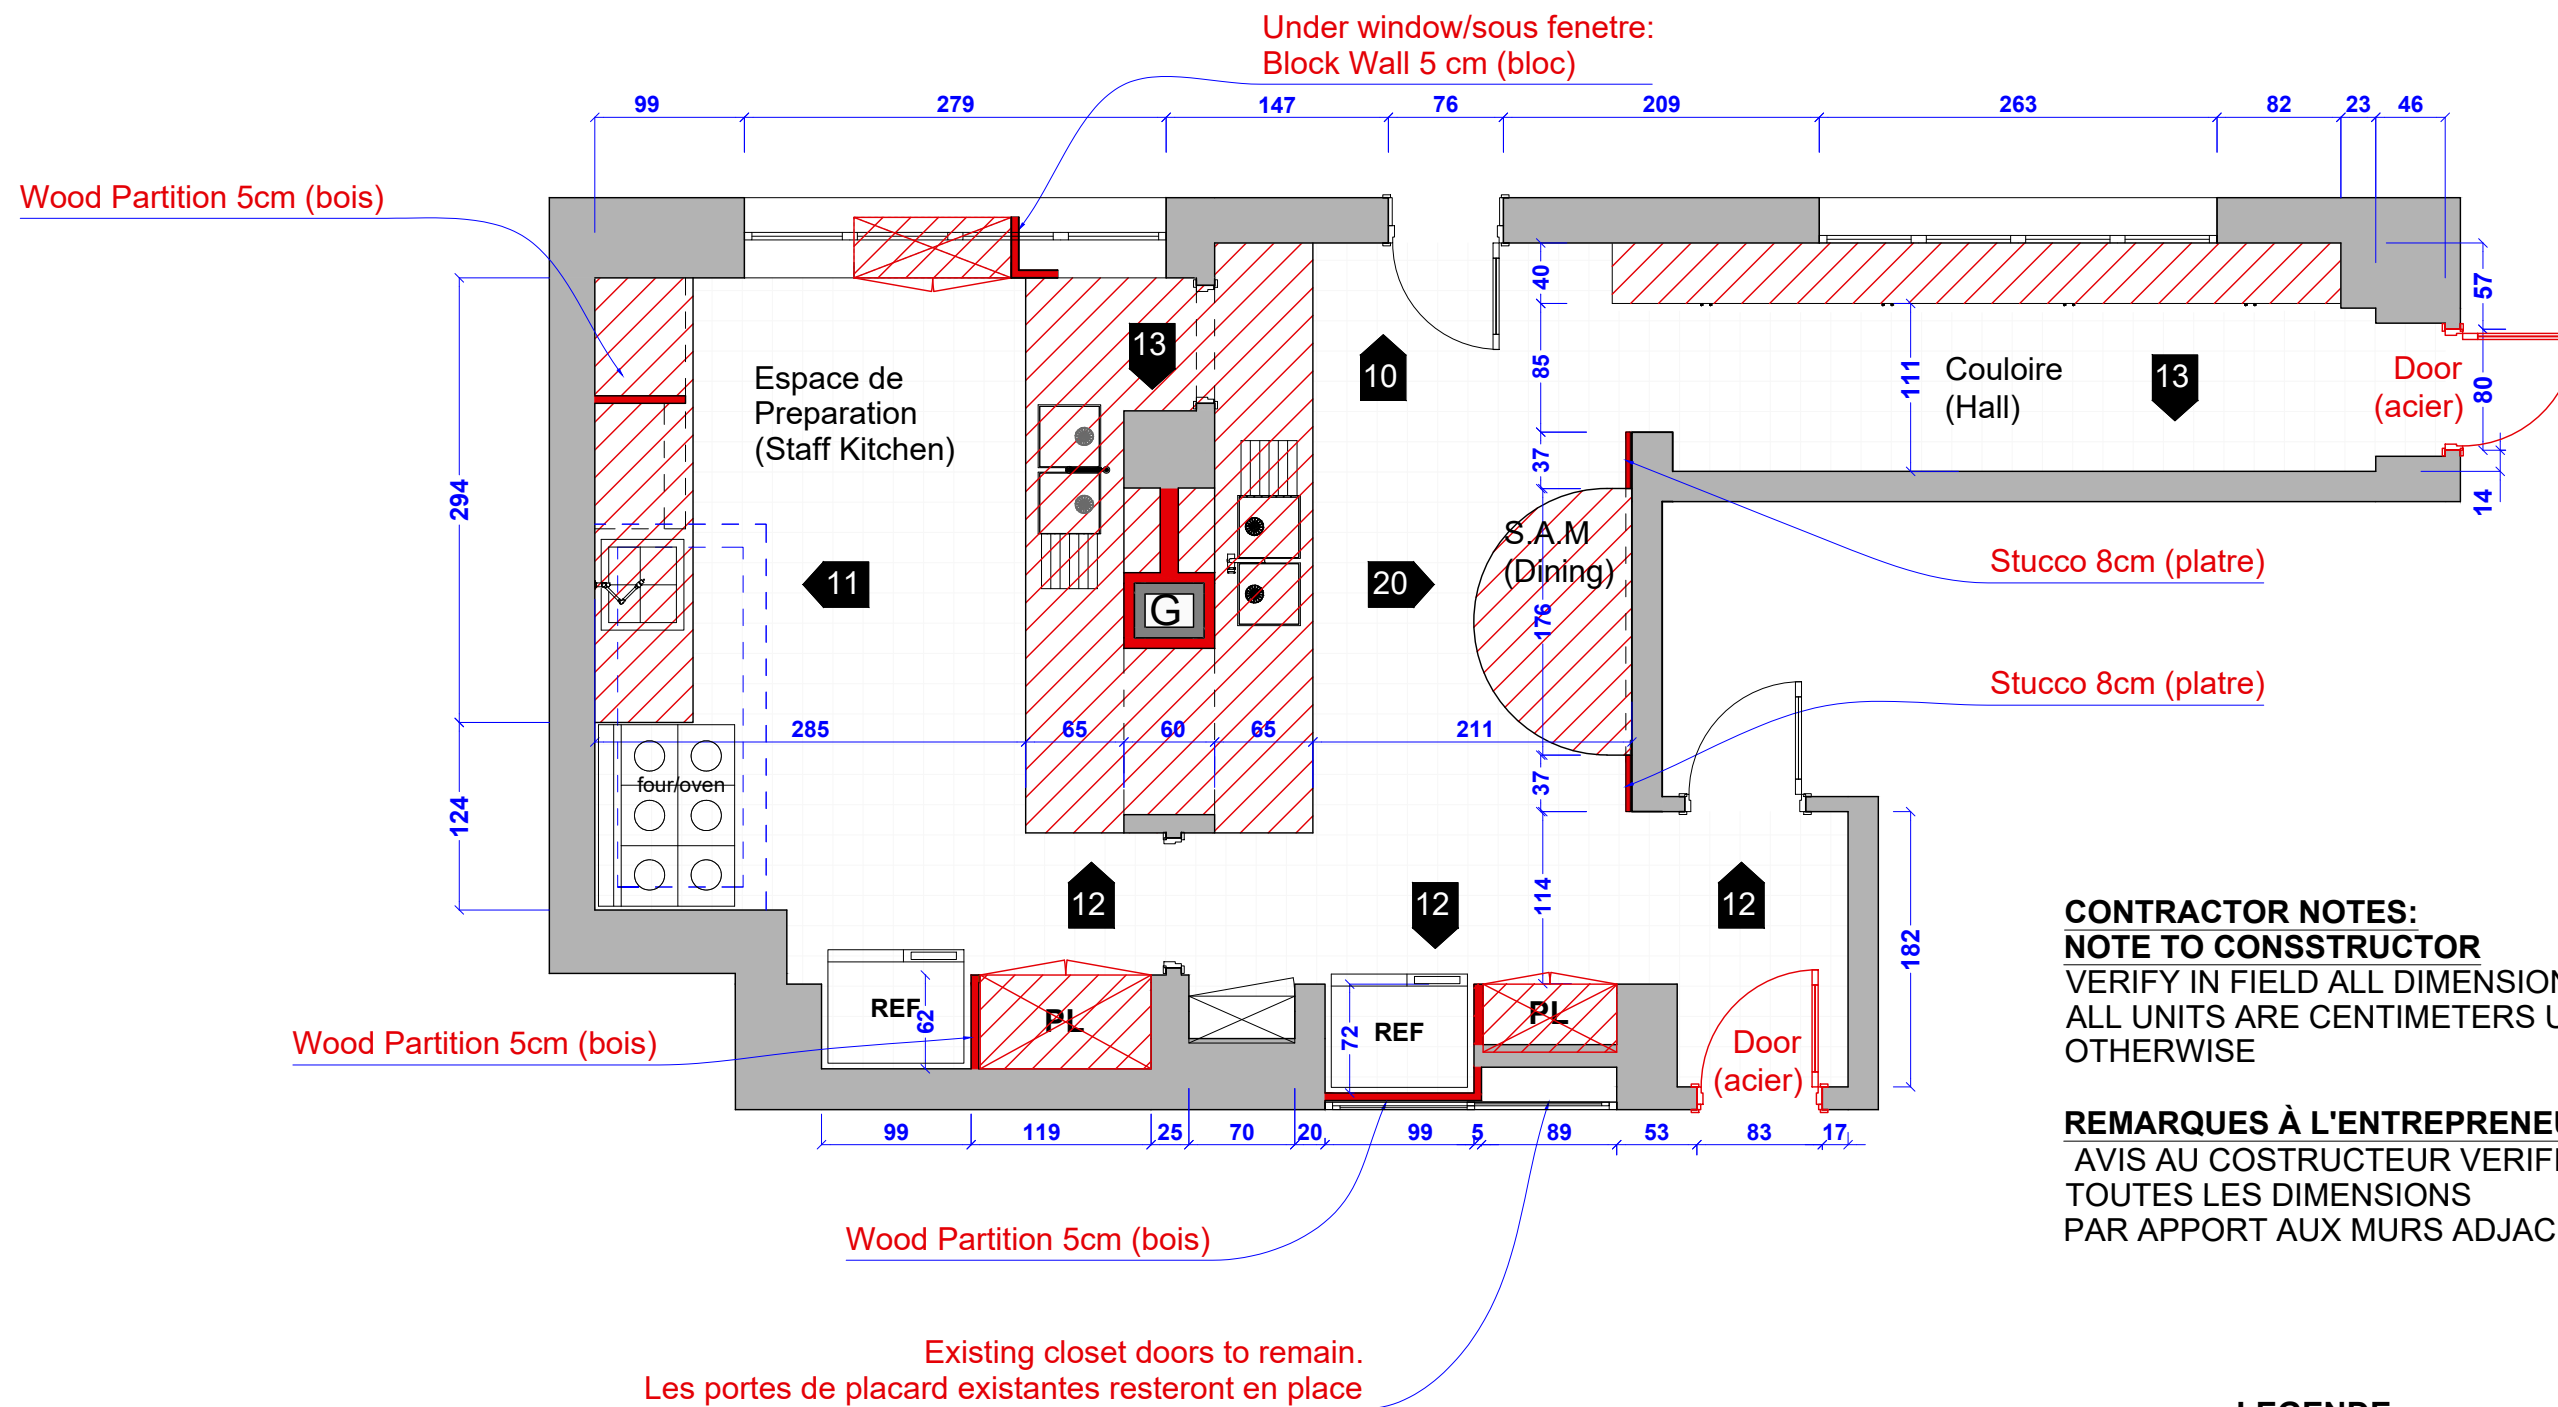

CONTRACTOR NOTES:
NOTE TO CONSTRUCTOR
VERIFY IN FIELD ALL DIMENSIONS TO ADJACENT WALLS
ALL UNITS ARE CENTIMETERS UNLESS NOTED
OTHERWISE

REMARQUES À L'ENTREPRENEUR :
AVIS AU COSTRUCTEUR VERIFIER SUR CHANTIER
TOUTES LES DIMENSIONS
PAR APPORT AUX MURS ADJACENTS

LEGENDE

	Mur a construire	New partition
	Table a construire	New millwork
	Porte a construire (2)	New Doors (2)

MAITRE D'OUVRAGE: / OWNER
CONSUL GENERAL CASABLANCA

PROJET
RENOVATION CUISINE / KICHEN RENOVATION


PHASE
2 FEB 2026 -100% -FOR BID

Construction Plan
Plan a construire

ECHELLE/SCALE
1/50

A359

Brian Coffman - A359 sarl
Appt. 6, Imm 38 Av. Youssef Ben Tachfine, Rabat 10000
Tél : +212 671 159 257
E-mail : bcoffman@architecture359.com
Web : www.architecture359.ma

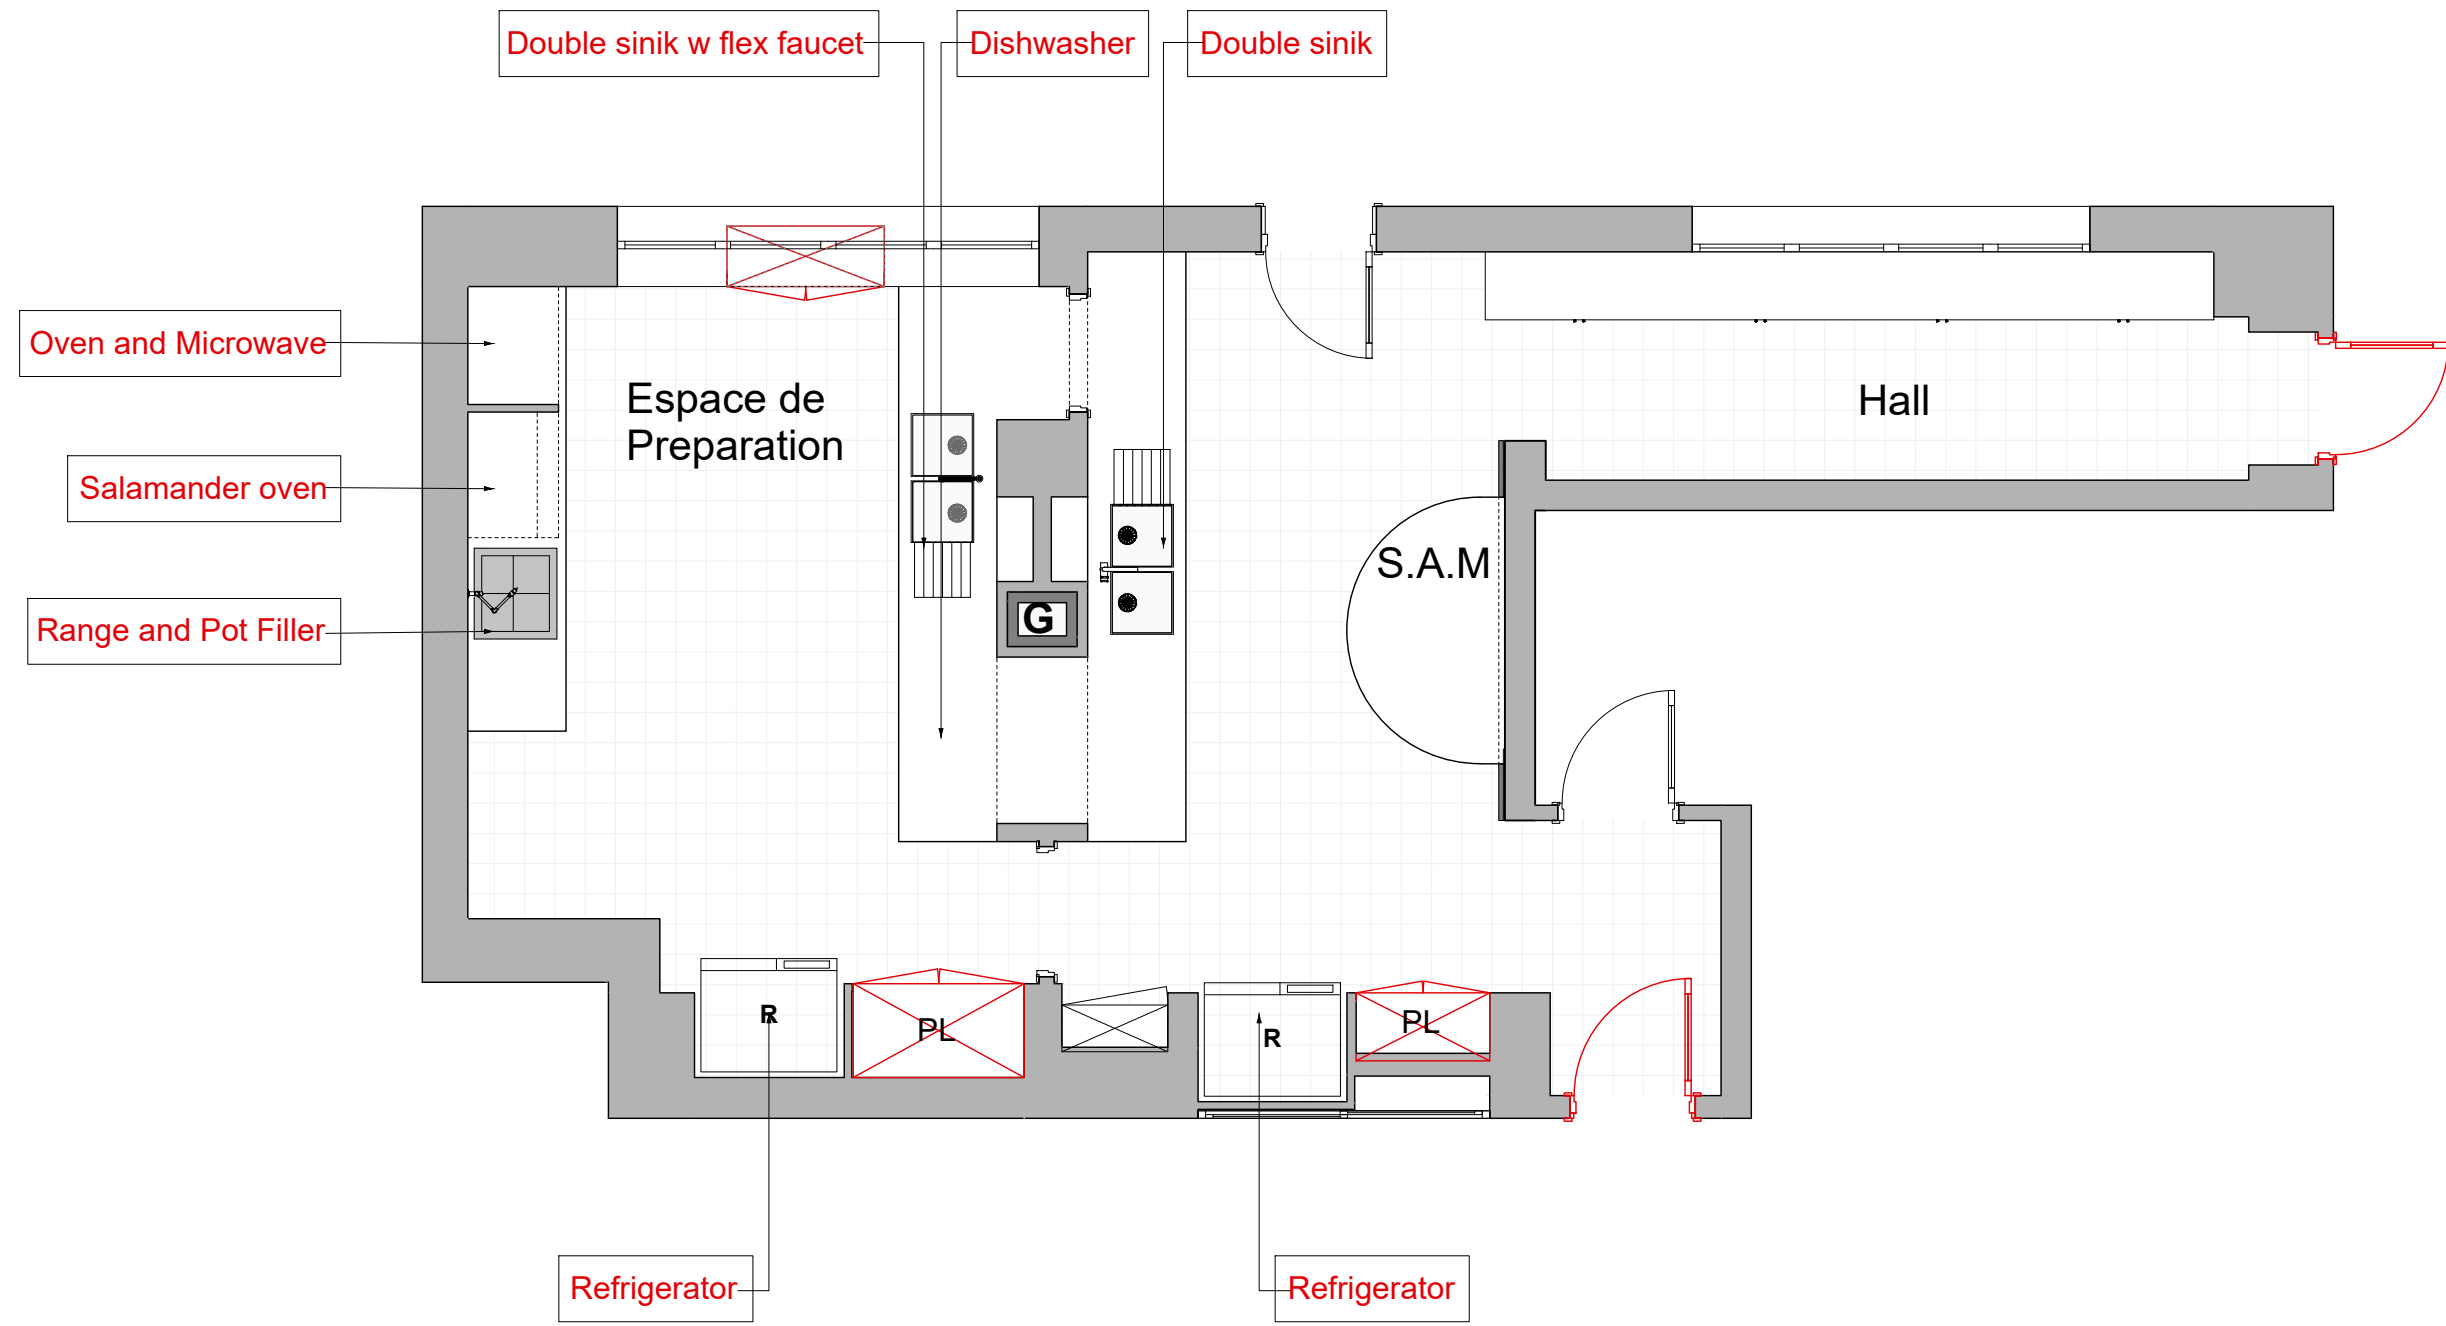

Contractor Notes

1. Contractor to follow all product manufacturers' recommendations for installation and surface preparation.


1. Le constructeur doit suivre toutes les recommandations des fabricants de produits pour l'installation et la préparation de la surface.

2. Install T1 floor tile under all cabinets and counters.

2. Installez des carreaux de sol T1 sous toutes les armoires et tous les comptoirs.

3. All walls to be painted P1 unless noted otherwise.
All walls to have tile base T2 unless noted otherwise.

3. Tous les murs doivent être peints P1 sauf indication contraire.
Tous les murs doivent avoir une base en carrelage T2 sauf indication contraire

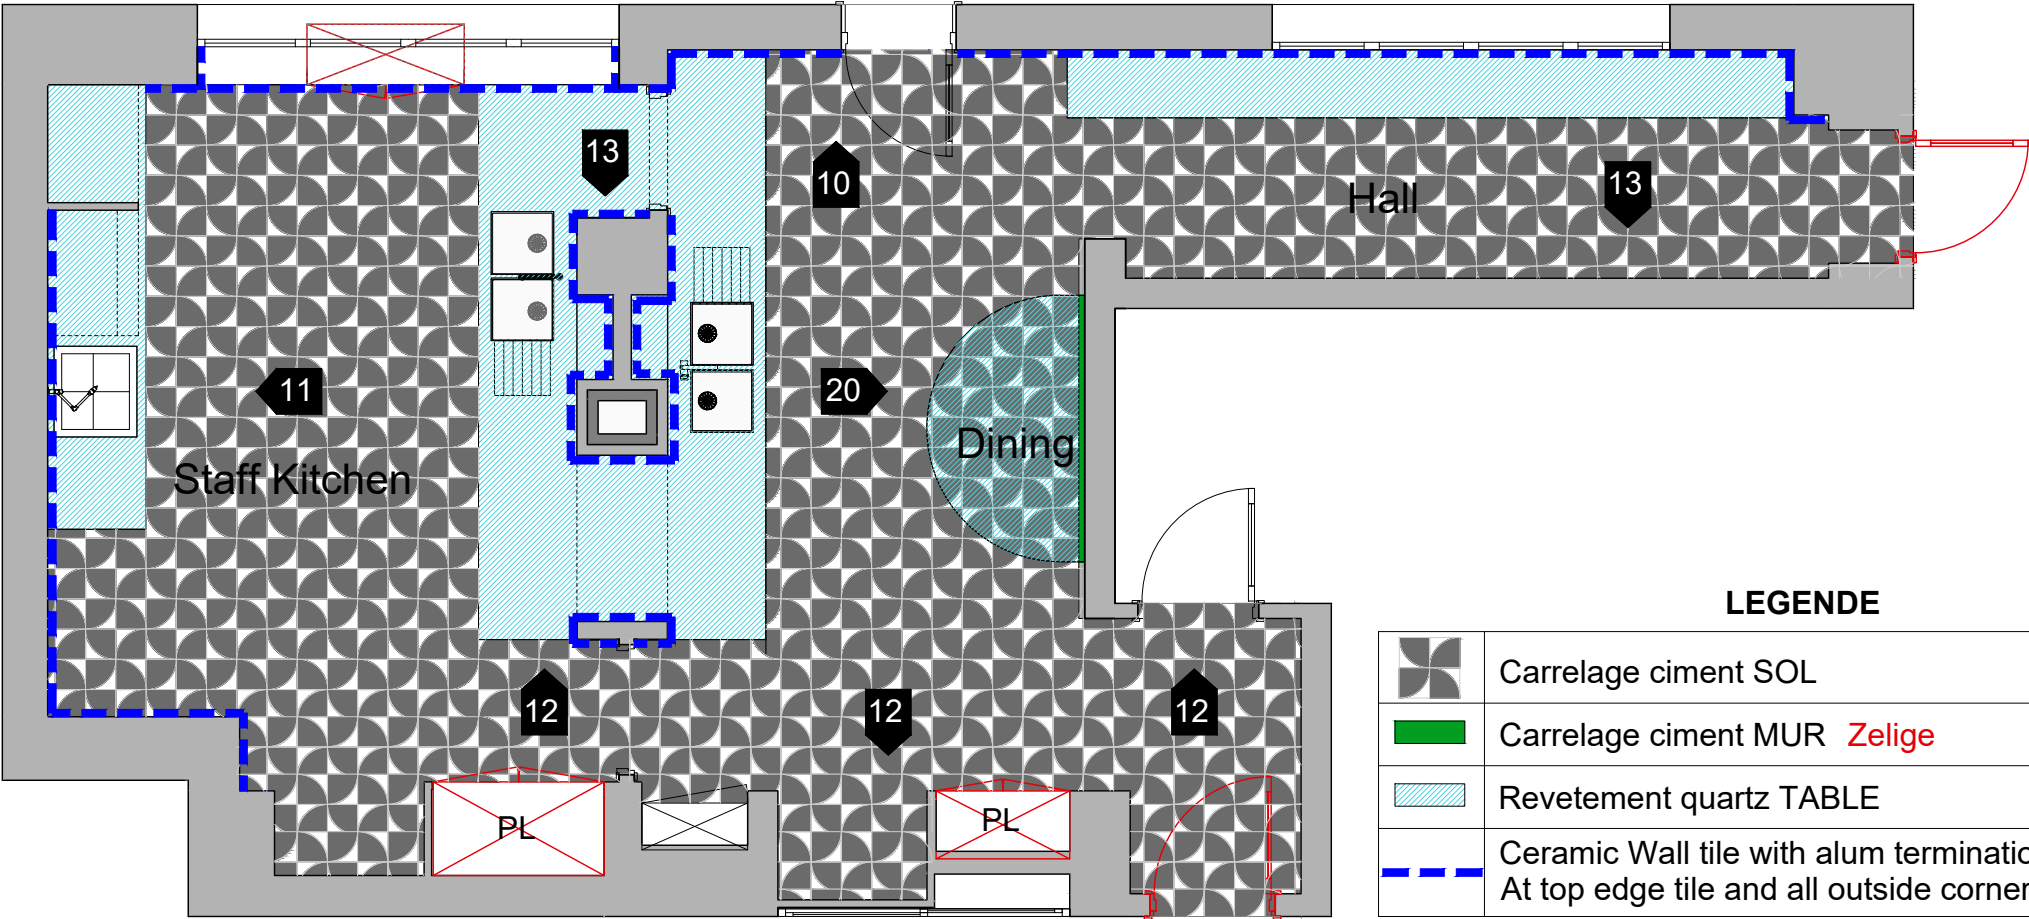

LEGENDE		
	Carrelage ciment SOL	T1
	Carrelage ciment MUR <i>Zelige</i>	T4
	Revetement quartz TABLE	Q
	Ceramic Wall tile with alum termination edge (baguettes) At top edge tile and all outside corners	T3

See Finish Schedule Voir Liste de Revetements



MAITRE D'OUVRAGE: / OWNER
CONSUL GENERAL CASABLANCA

PROJET
RENOVATION CUISINE / KICHEN RENOVATION

PHASE
2 FEB 2026 -100% -FOR BID


Elevations



ECHELLE/SCALE
1/50

A359

Brian Coffman - A359 sarlau
Appt. 6, Imm 38 Av. Youssef Ben Tachfine, Rabat 10000
Tél : +212 671 159 257
E-mail : bcoffman@architecture359.com
Web : www.architecture359.ma

10

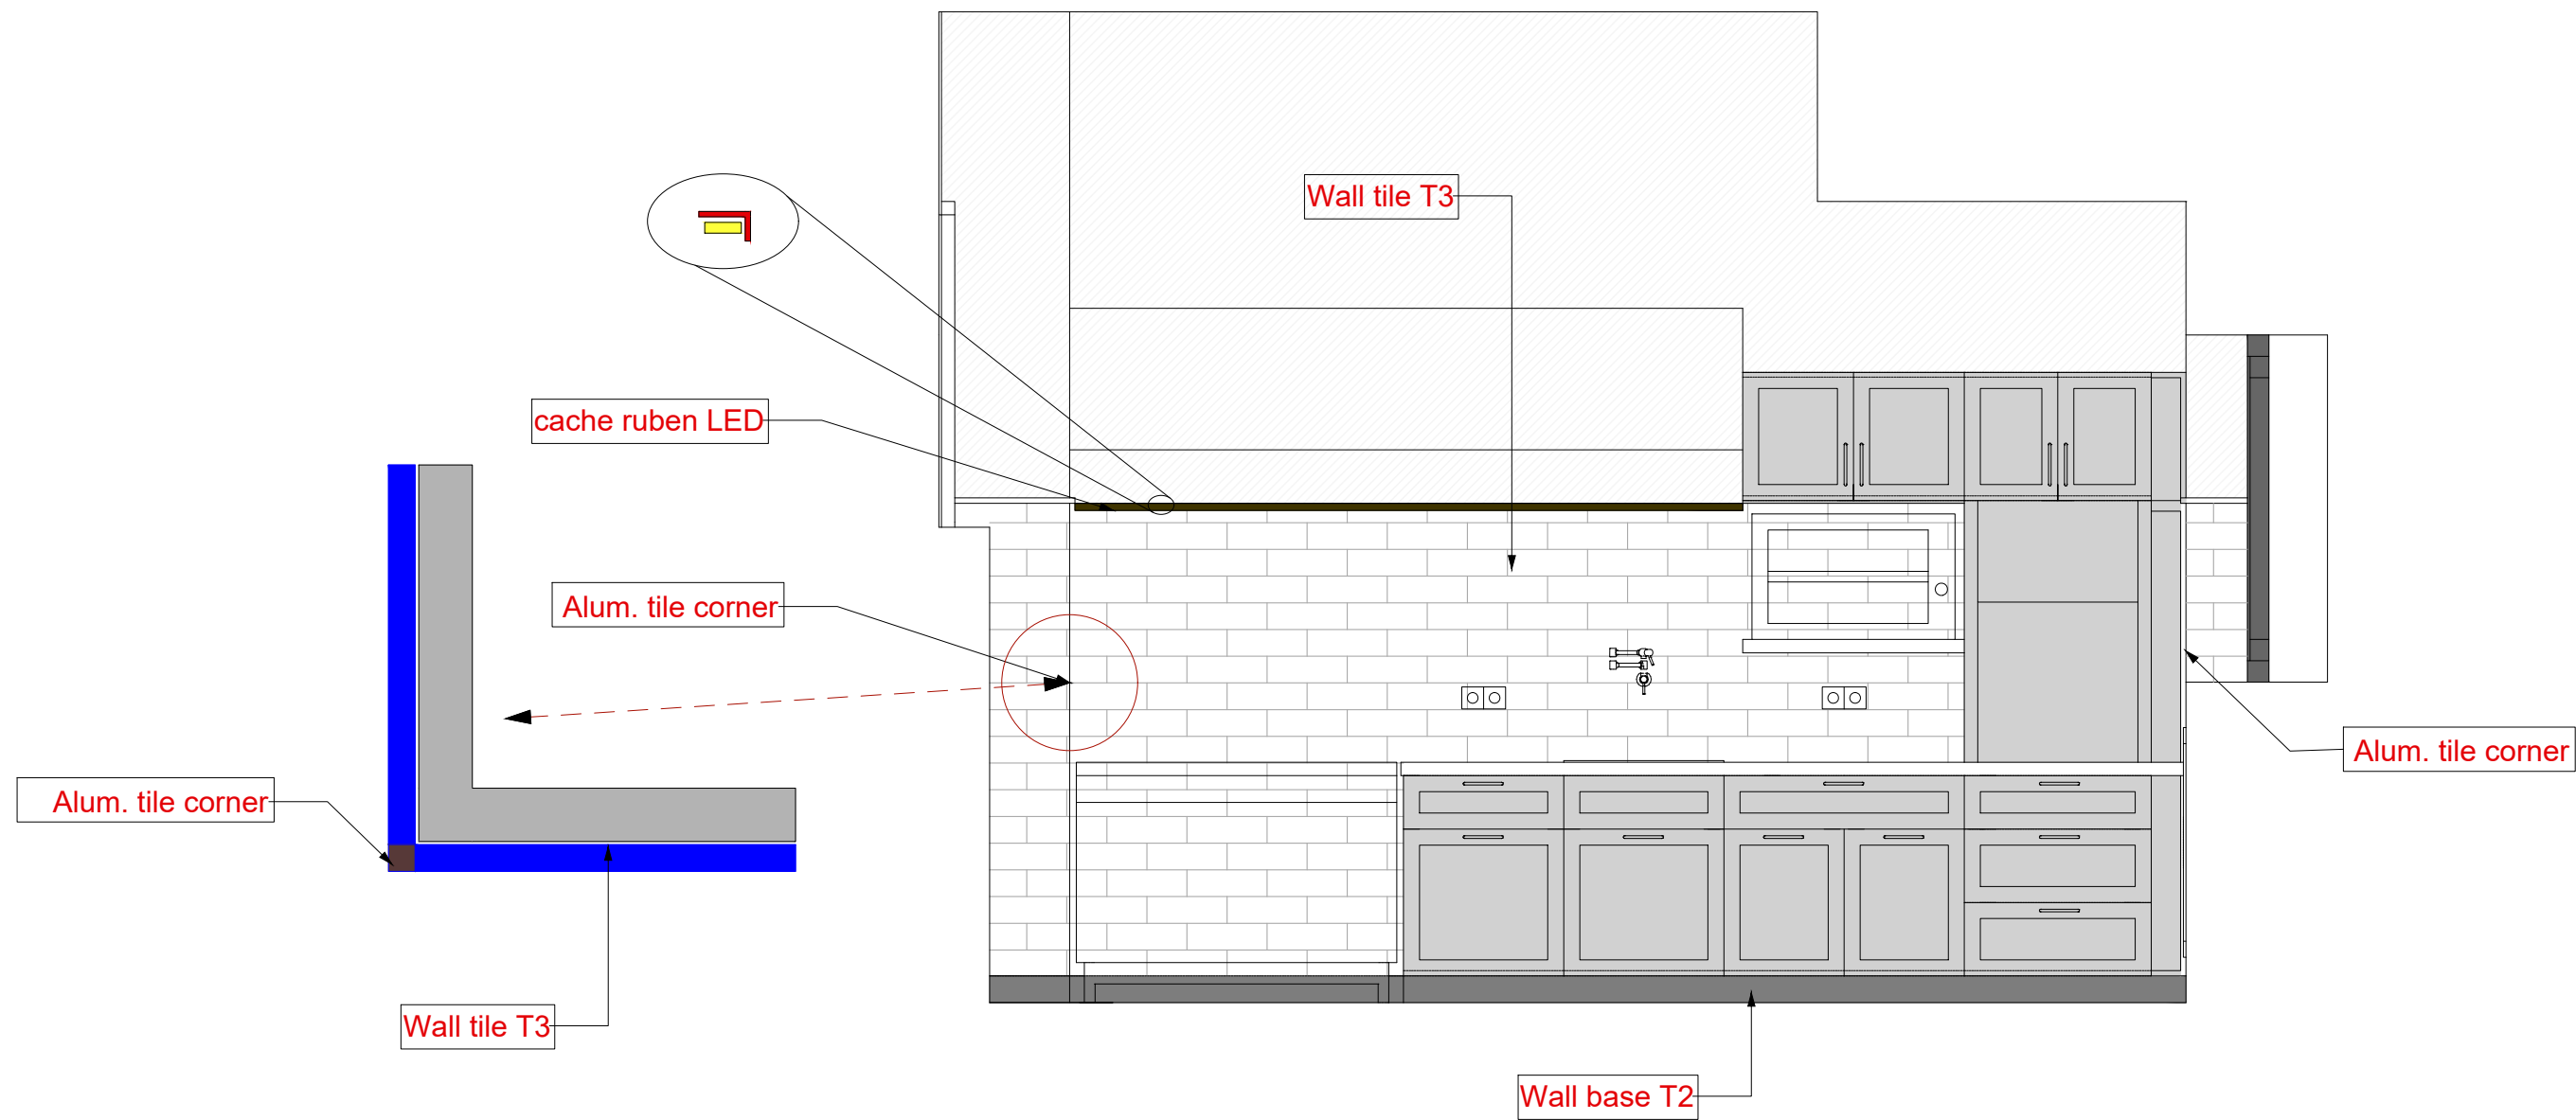

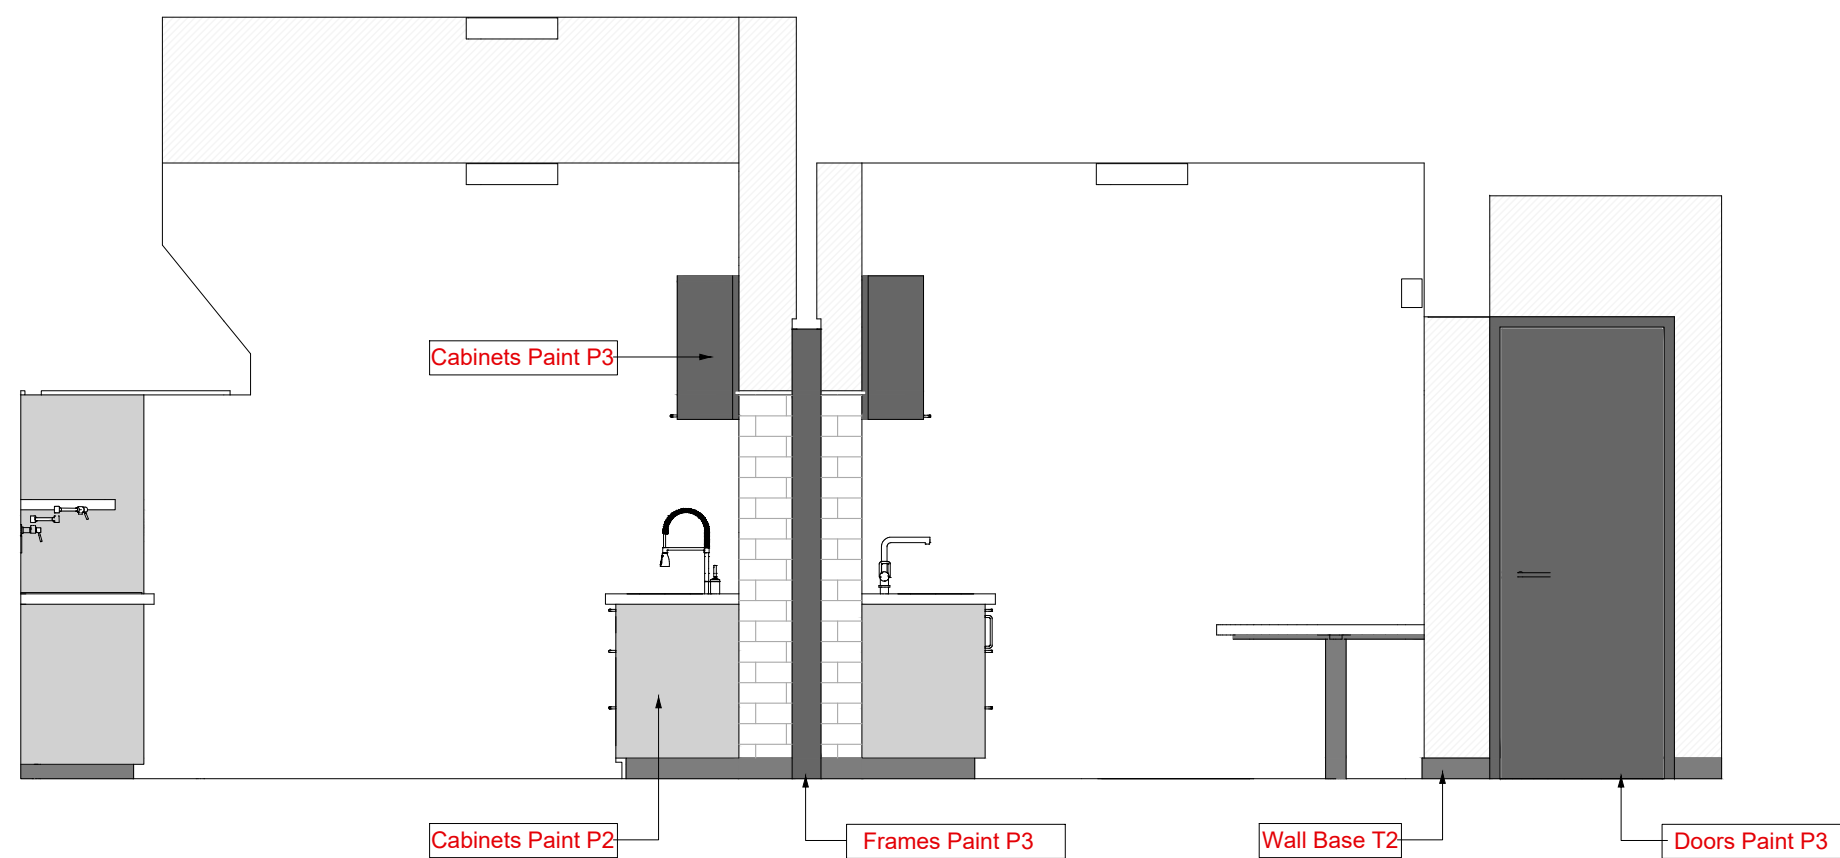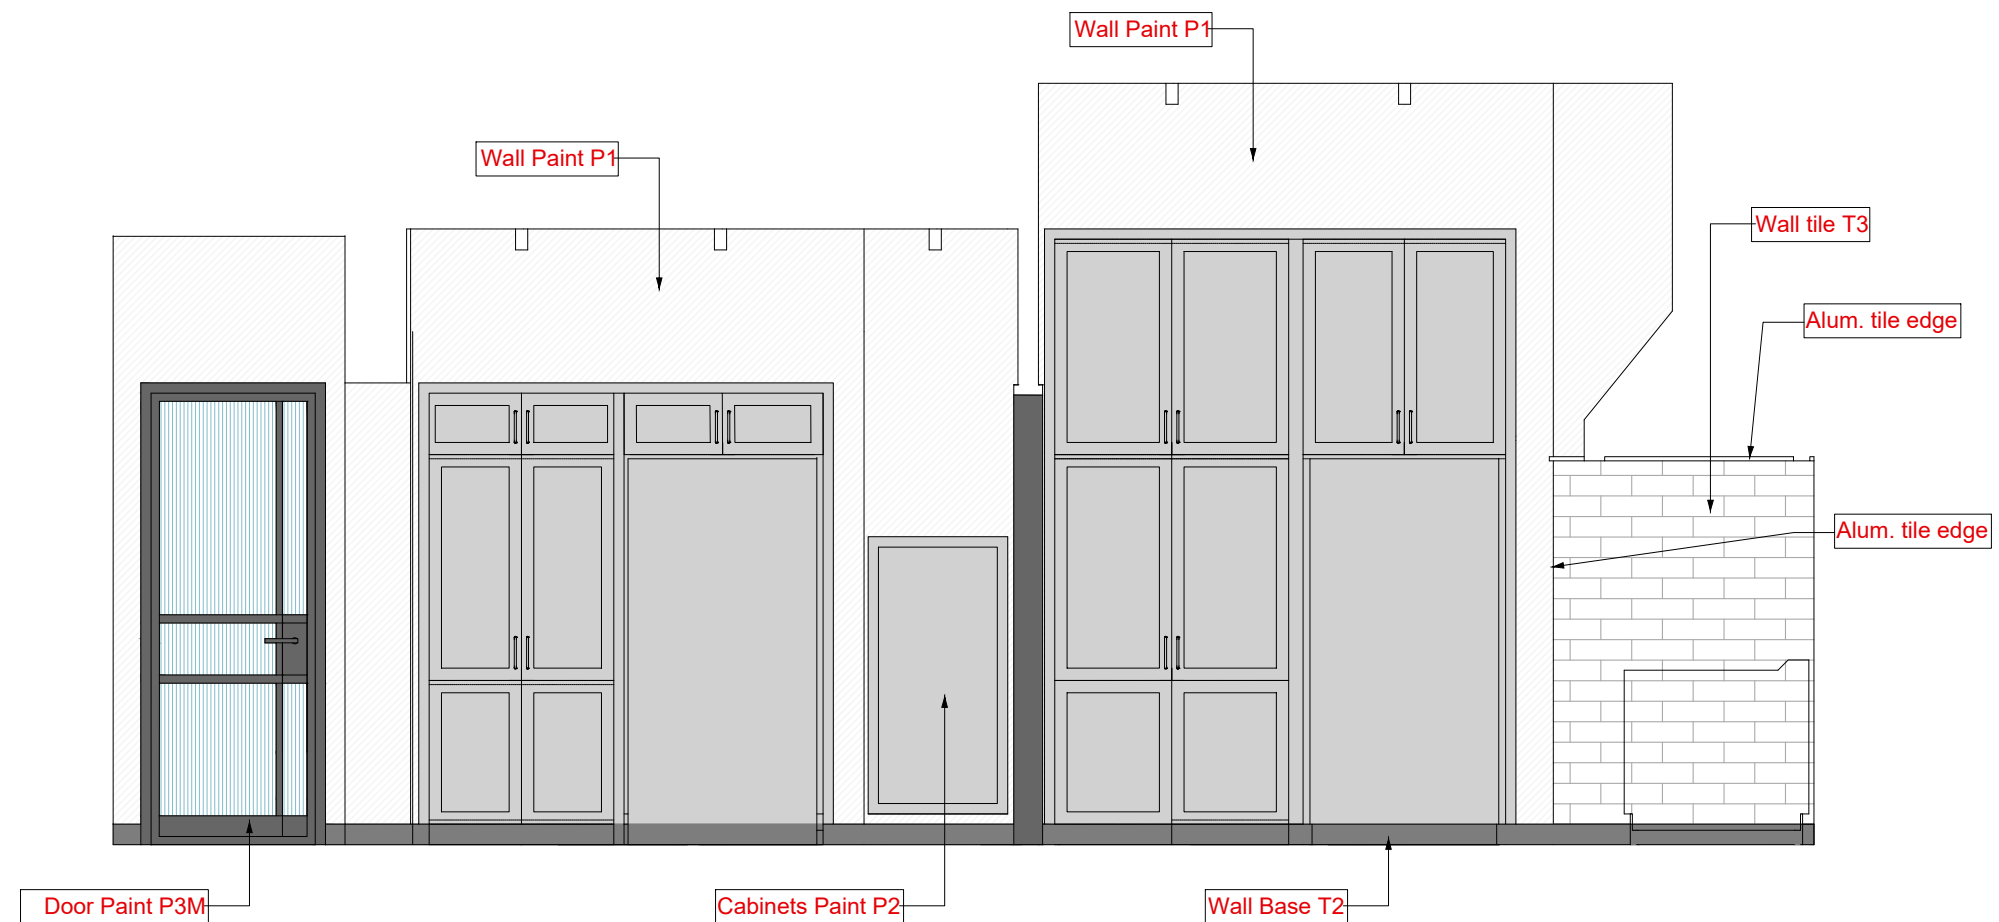

MAITRE D'OUVRAGE: / OWNER
CONSUL GENERAL CASABLANCA

PROJET
RENOVATION CUISINE / KICHEN RENOVATION

PHASE
2 FEB 2026 -100% -FOR BID


Elevations


ECHELLE/SCALE
1/50

A359

Brian Coffman - A359 sarlau
Appt. 6, Imm 38 Av. Youssef Ben Tachfine, Rabat 10000
Tél : +212 671 159 257
E-mail : bcoffman@architecture359.com
Web : www.architecture359.ma

12

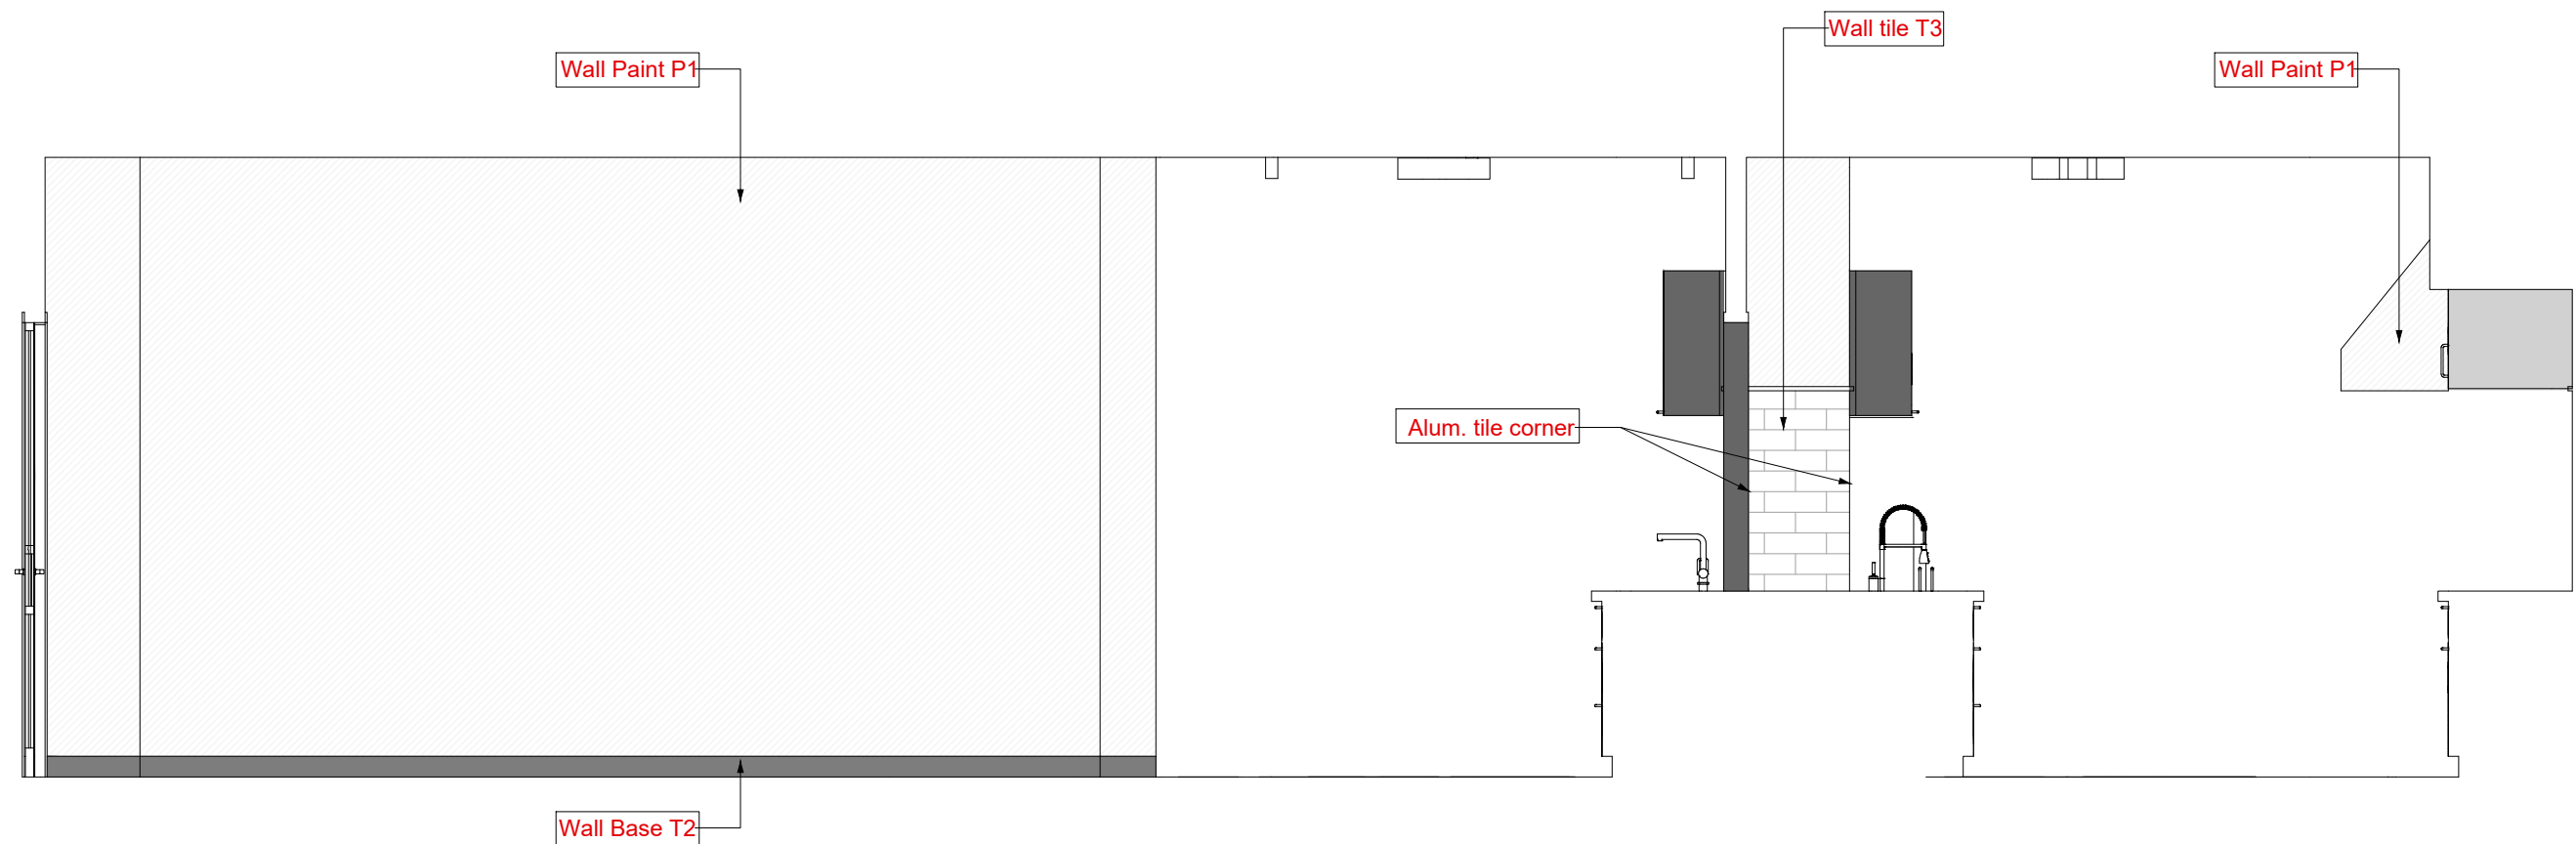

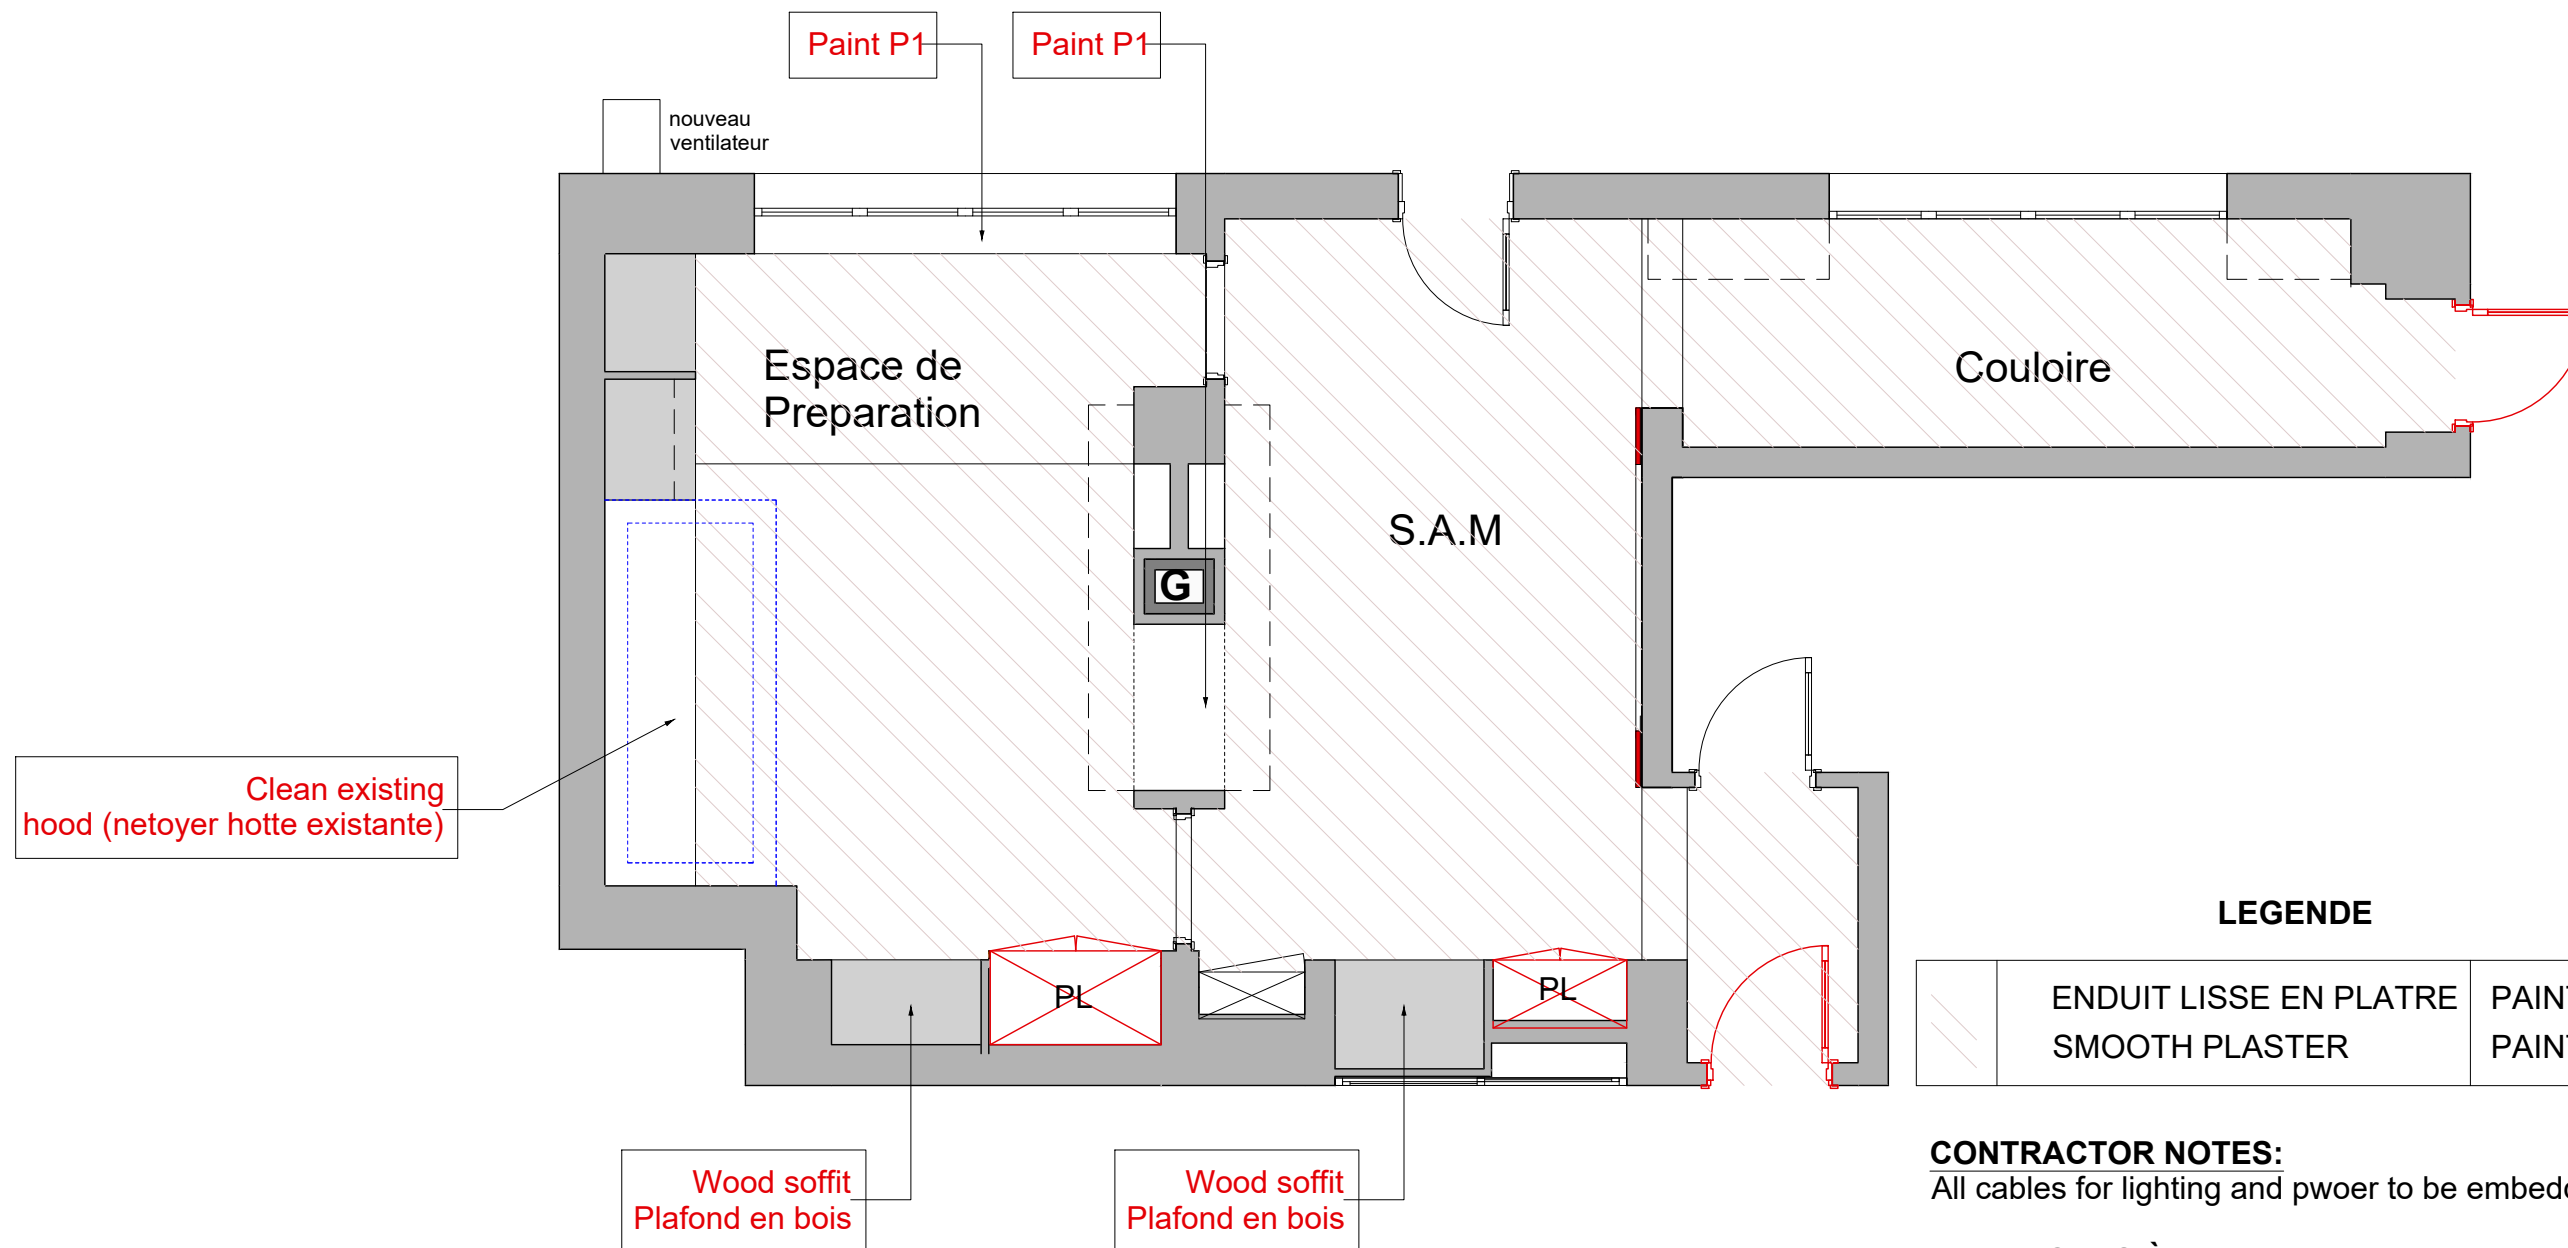



LEGENDE

	ENDUIT LISSE EN PLATRE SMOOTH PLASTER		PAINT P1 PAINT P1
--	--	--	----------------------

CONTRACTOR NOTES:
All cables for lighting and pwoer to be embedded in plaster

REMARQUES À L'ENTREPRENEUR :
Tous les câbles d'éclairage et d'alimentation doivent être encastrés dans le plâtre

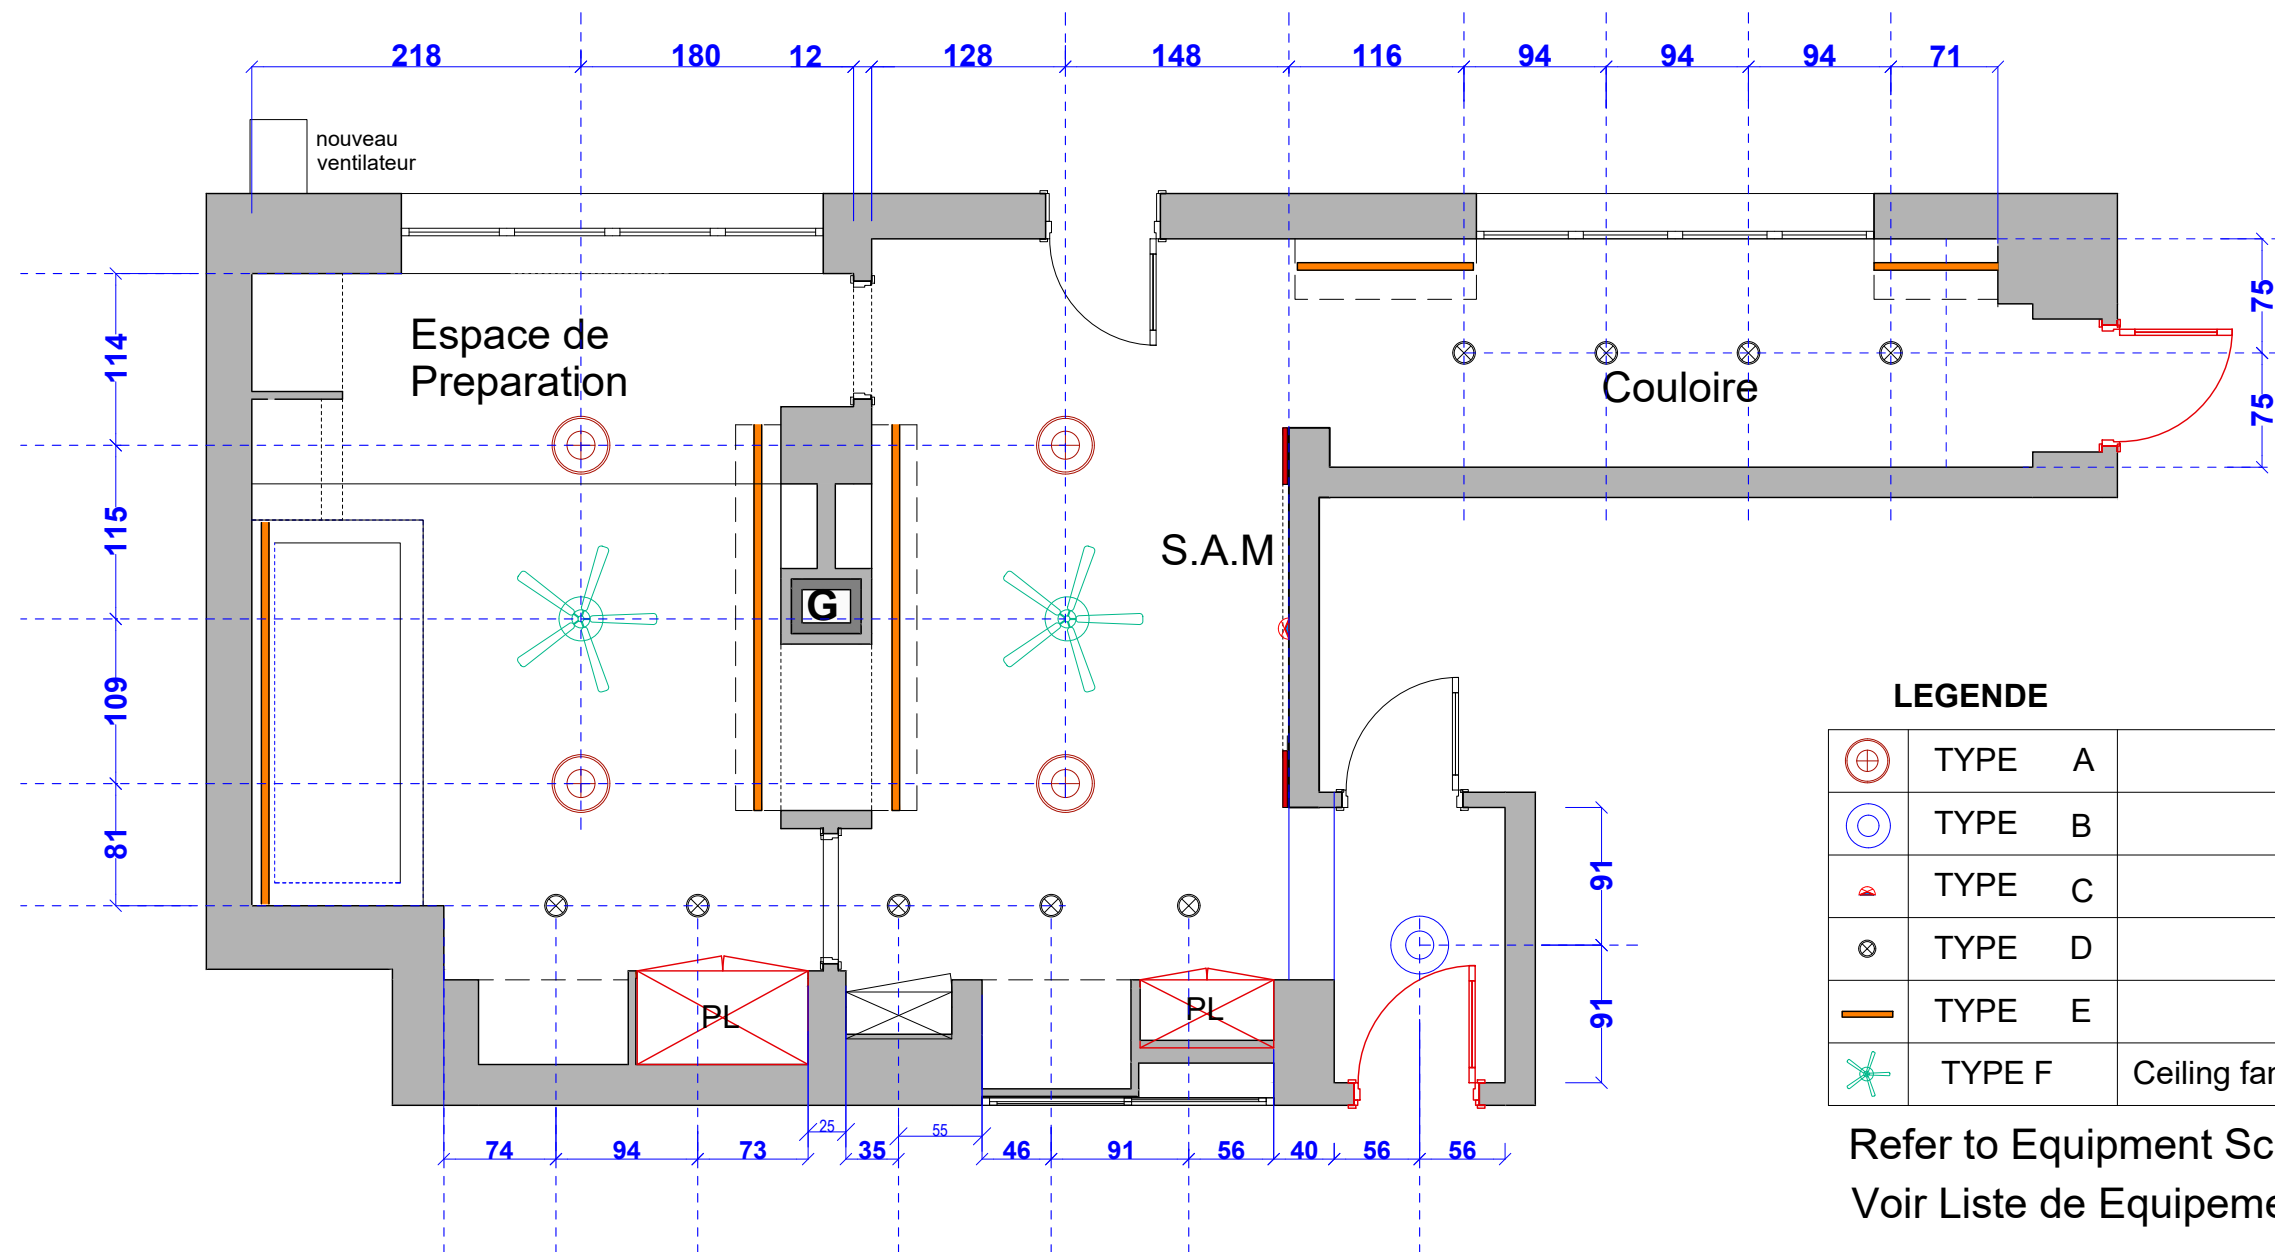

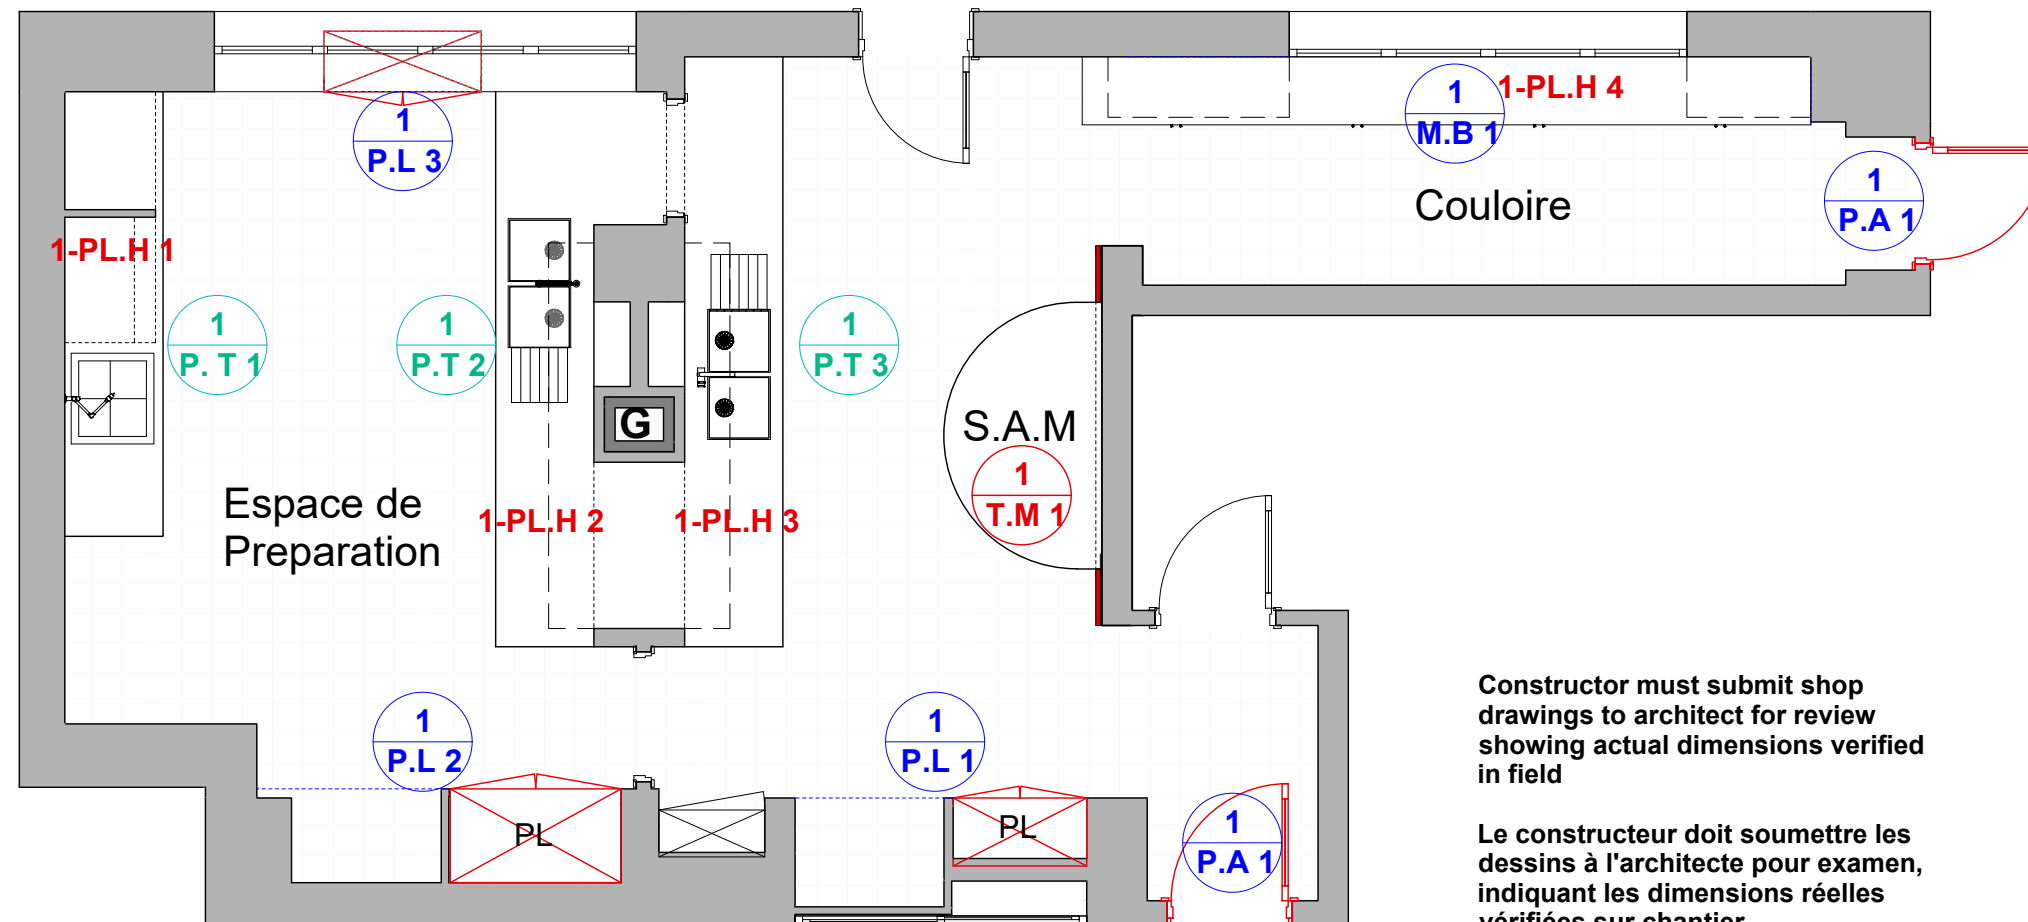

Constructor must submit shop drawings to architect for review showing actual dimensions verified in field

Le constructeur doit soumettre les dessins à l'architecte pour examen, indiquant les dimensions réelles vérifiées sur chantier.

REPERAGE

1P.A 1



H:2,25
L:0,90

STEEL FRAME DOOR
PORTE EN ACIER
THERMOLAQUE GRIS

QUANTITE : 2

LOCALISATION :
CUISINE

N
O
M
E
N
C
L
A
T
U
R
E
&
D
E
T
A
I
L
S

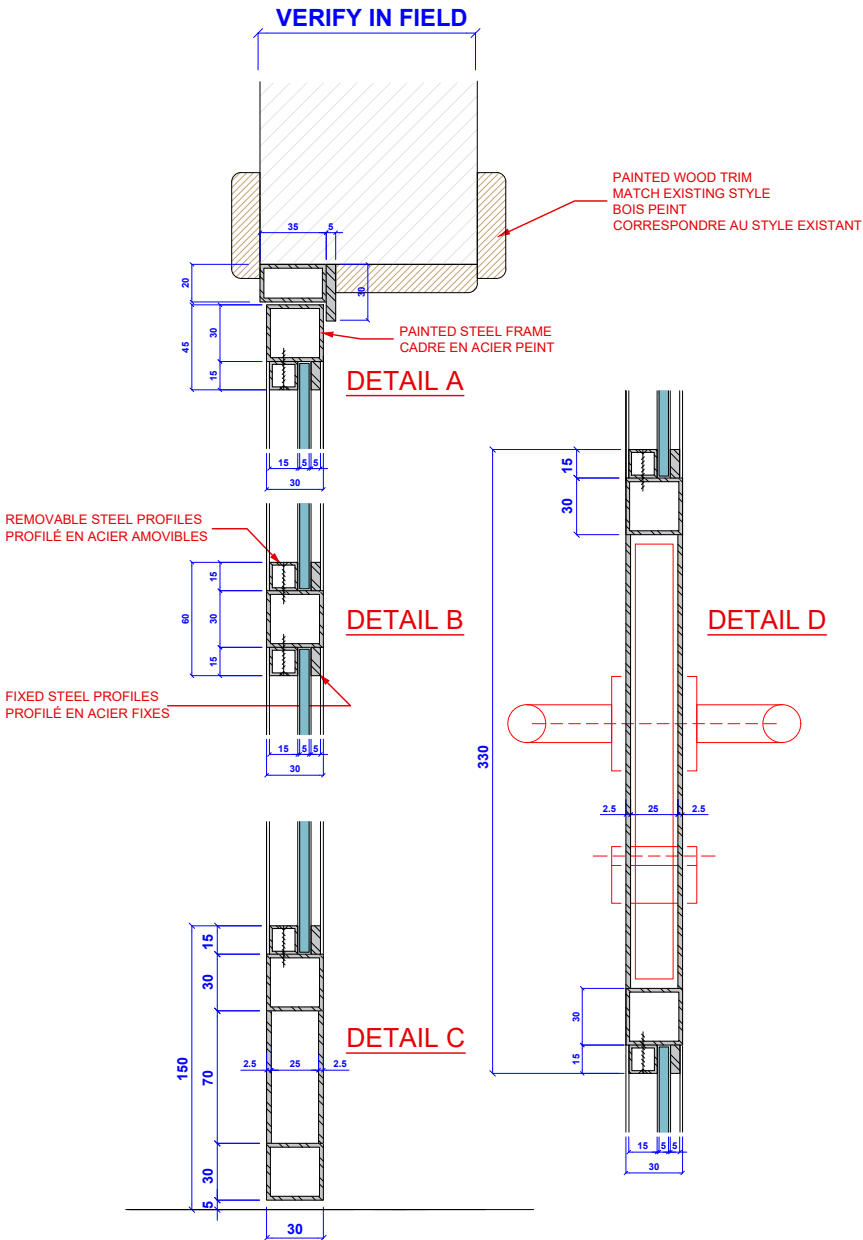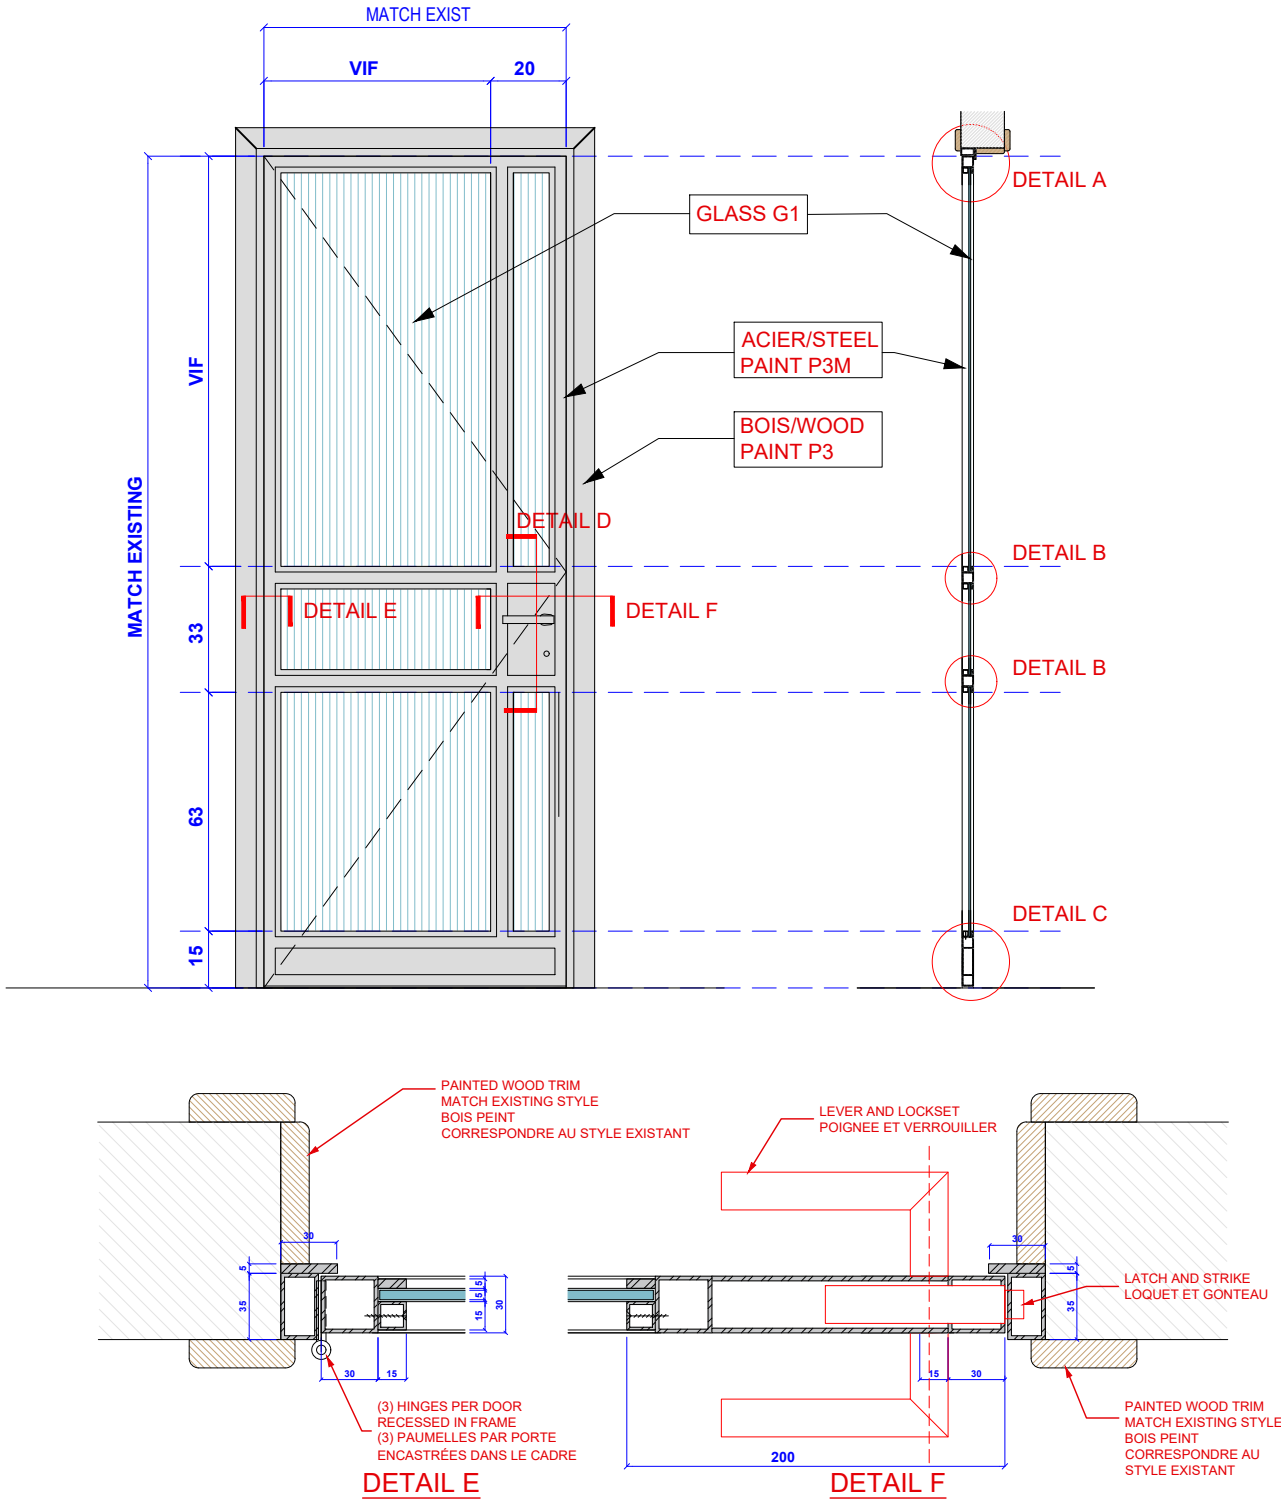

ALL GLASS RIBBED AND TEMPERED. TOUT VERRE CÔTELÉ ET TREMPÉ
ALL JOINTS WELDED AND GROUND SMOOTH. TOUS LES JOINTS SONT SOUDÉS ET MEULÉS LISSES.

HUISSERIE	CADRE EN ACIER / STEEL GAMME PROFIL SEE DETAIL FOR PROFILE VER DETAILLE
VANTAIL	1 OUVRANT A LA FRANCAISE
QUINCAILLERIE	6 PAUMELLES 140 x 80 NOIR INVISIBLES EN INOX, 2 POIGNEES NOIR, AU CHOIX DE L'ARCHITECTE
FINITION	PAINT P3

Constructor must submit shop drawings to architect for review
showing actual dimensions verified in field

Le constructeur doit soumettre les dessins à l'architecte pour
examen, indiquant les dimensions réelles vérifiées sur chantier.

MAITRE D'OUVRAGE: / OWNER
CONSUL GENERAL CASABLANCA

PROJET
RENOVATION CUISINE / KICHEN RENOVATION

PHASE
2 FEB 2026 -100% -FOR BID

Detaille menuiserie
Millwork Detail

ECHELLE/SCALE
1/20

A359

Brian Coffman - A359 sarl
Appt. 6, Imm 38 Av. Youssef Ben Tachfine, Rabat 10000
Tél : +212 671 159 257
E-mail : bcoffman@architecture359.com
Web : www.architecture359.ma

REPERAGE

1-MB. 1

PLAN TRAVAIL
0,45 X 2,82 X 0,90


MEUBLE BAS

QUANTITE : 1


LOCALISATION :

CUISINE

N
O
M
E
N
C
L
A
T
U
R
E
&
D
E
T
A
I
L
S

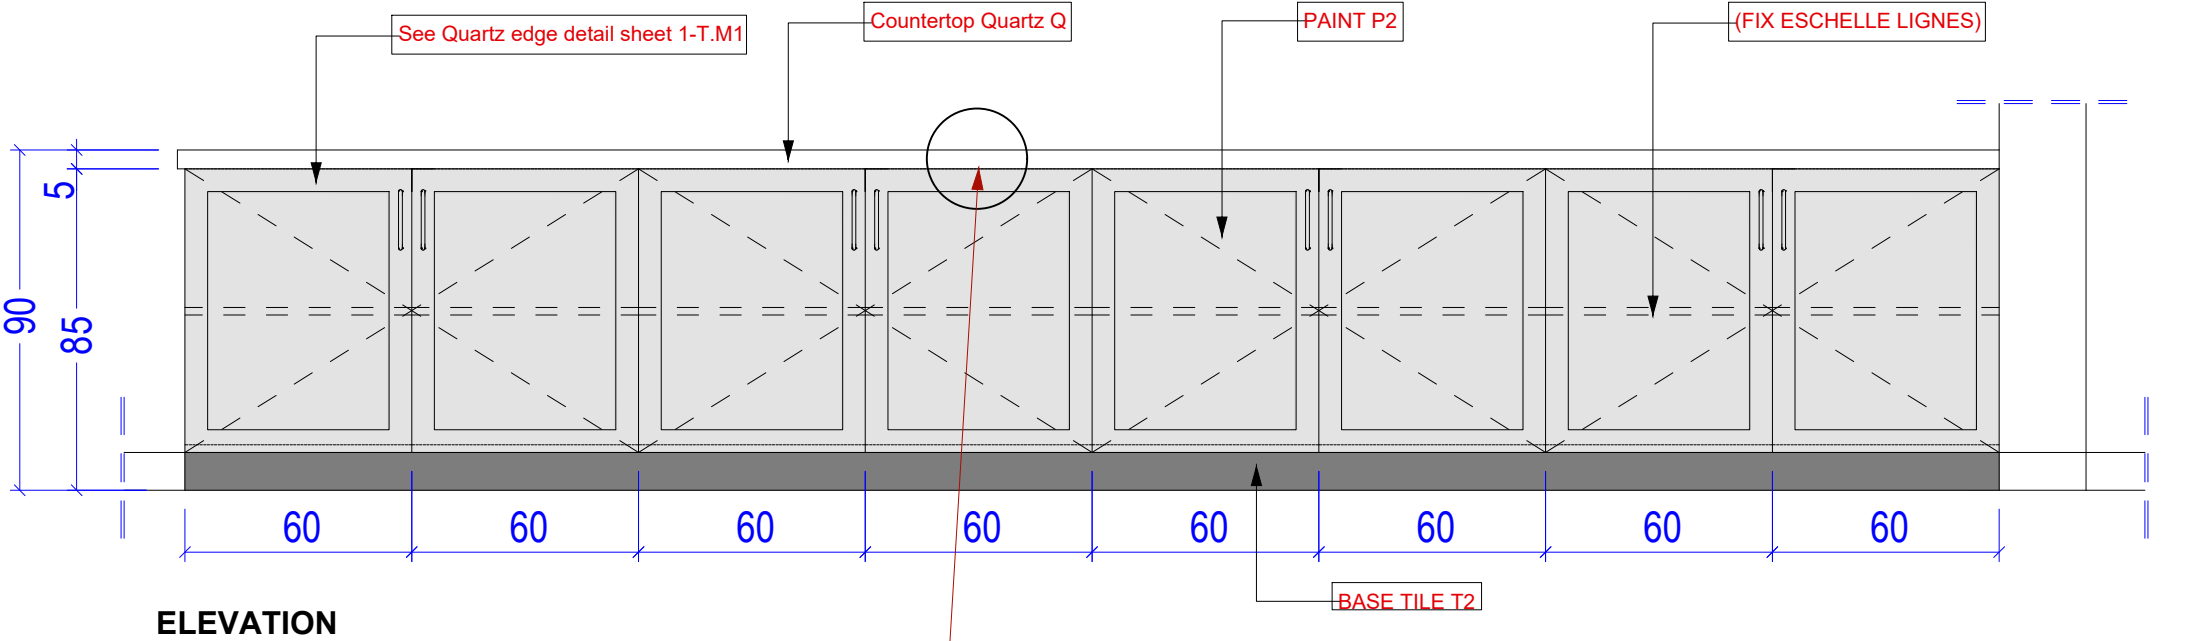


ELEVATION

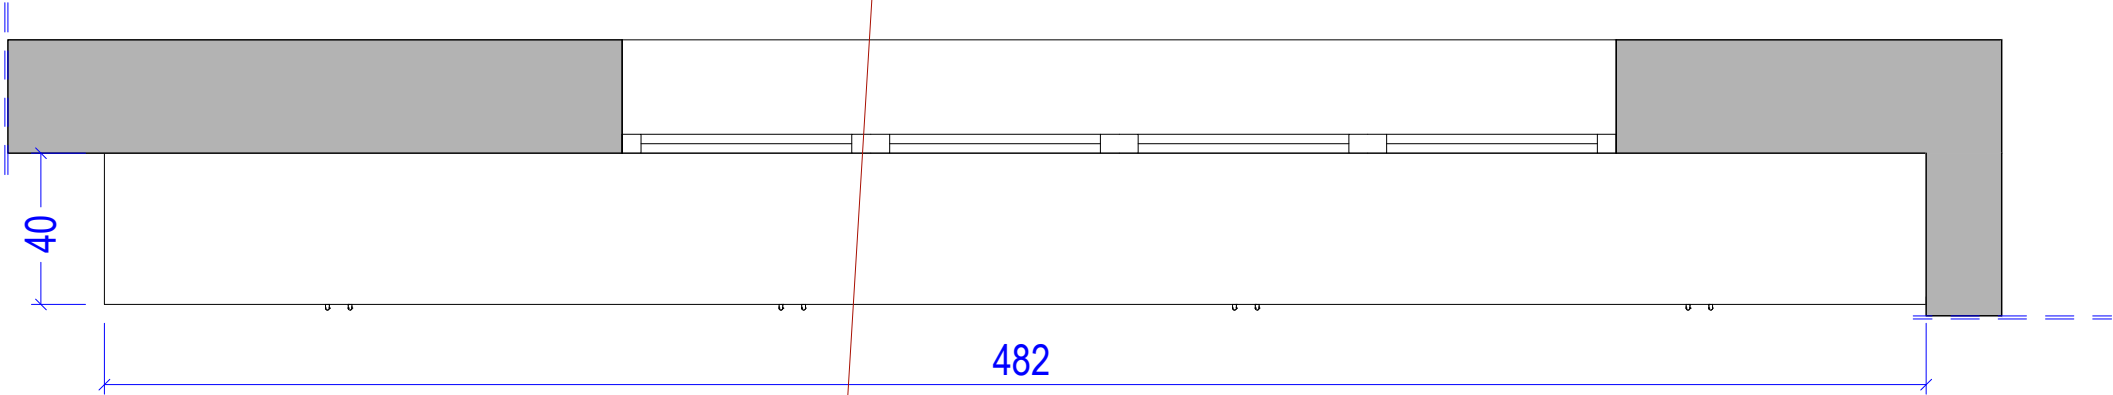

VUE EN PLAN

DETAIL

Quartz edge detail all countertops
Détails des bords en quartz
continuous pattern across joint.
motif continu sur l'articulation

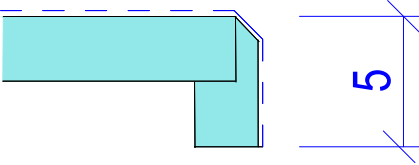

Adjustable shelves, all units
Étagères réglables, toutes les meubles



HUISSERIE	CADRE EN BOIS PORTE METALLIQUE VITREE SABLEE	Constructor must submit shop drawings to architect for review showing actual dimensions verified in field Le constructeur doit soumettre les dessins à l'architecte pour examen, indiquant les dimensions réelles vérifiées sur chantier.
VANTAIL	5 OUVRANT A LA FRANCAISE	
QUINCAILLERIE	10 PAUMELLES 140 x 80 CHROMEES INVISIBLES EN INOX, 5 POIGNEES EN INOX, AU CHOIX DE L'ARCHITECTE	
FINITION	BOIS HETRE PEINTURE COULEUR GRIS NOIR AU CHOIX DE L'ARCHITECTE	

MAITRE D'OUVRAGE: / OWNER
CONSUL GENERAL CASABLANCA

PROJET
RENOVATION CUISINE / KICHEN RENOVATION

PHASE
2 FEB 2026 -100% -FOR BID

Detaille menuiserie
Millwork Detail

ECHELLE/SCALE
1/20

A359

Brian Coffman - A359 sarl
Appt. 6, Imm 38 Av. Youssef Ben Tachfine, Rabat 10000
Tél : +212 671 159 257
E-mail : bcoffman@architecture359.com
Web : www.architecture359.ma

		REPERAGE	1-PL.H 4 PLAN TRAVAIL 0,45 X 0,80 X 1,55	PLACARD HAUT	QUANTITE : 1	
					LOCALISATION :	CUISINE
N O M E N C L A T U R E & D E T A I L S						
	ELEVATION VUE EN PLAN					
	HUISSERIE	CADRE EN BOIS PORTE METALLIQUE VITREE SABLEE				Constructor must submit shop drawings to architect for review showing actual dimensions verified in field
	VANTAIL	5 OUVRANT A LA FRANCAISE				
	QUINCAILLERIE	10 PAUMELLES 140 x 80 CHROMEES INVISIBLES EN INOX, 5 POIGNEES EN INOX, AU CHOIX DE L'ARCHITECTE				Le constructeur doit soumettre les dessins à l'architecte pour

MAITRE D'OUVRAGE: / OWNER CONSUL GENERAL CASABLANCA	PROJET RENOVATION CUISINE / KICHEN RENOVATION	PHASE 2 FEB 2026 -100% -FOR BID	Detaille menuiserie Millwork Detail	ECHELLE/SCALE 1/20	A359 Brian Coffman - A359 sarlau Appt. 6, Imm 38 Av. Youssef Ben Tachfine, Rabat 10000 Tél : +212 671 159 257 E-mail : bcoffman@architecture359.com Web : www.architecture359.ma	19
--	--	------------------------------------	--	-----------------------	---	----

REPERAGE

1-T.M1 P 105 x L 1.76 x H 0.75



TABLE A MANGER

QUANTITE : 1

LOCALISATION :

CUISINE

N
O
M
E
N
C
L
A
T
U
R
E
&
D
E
T
A
I
L
S

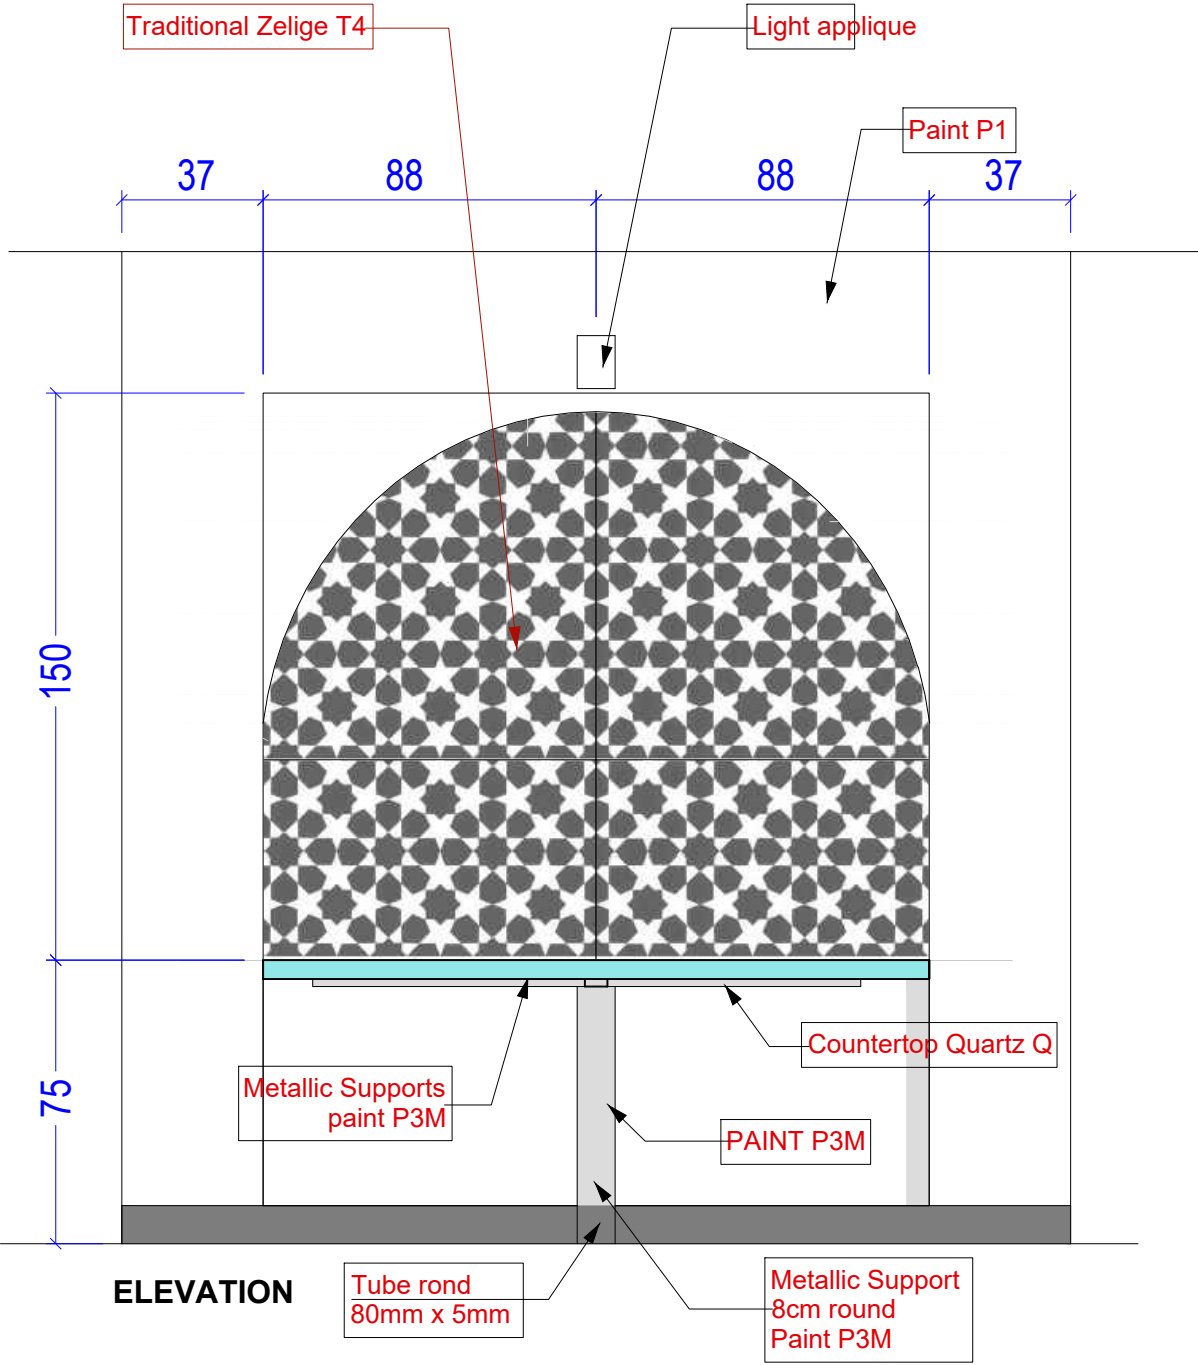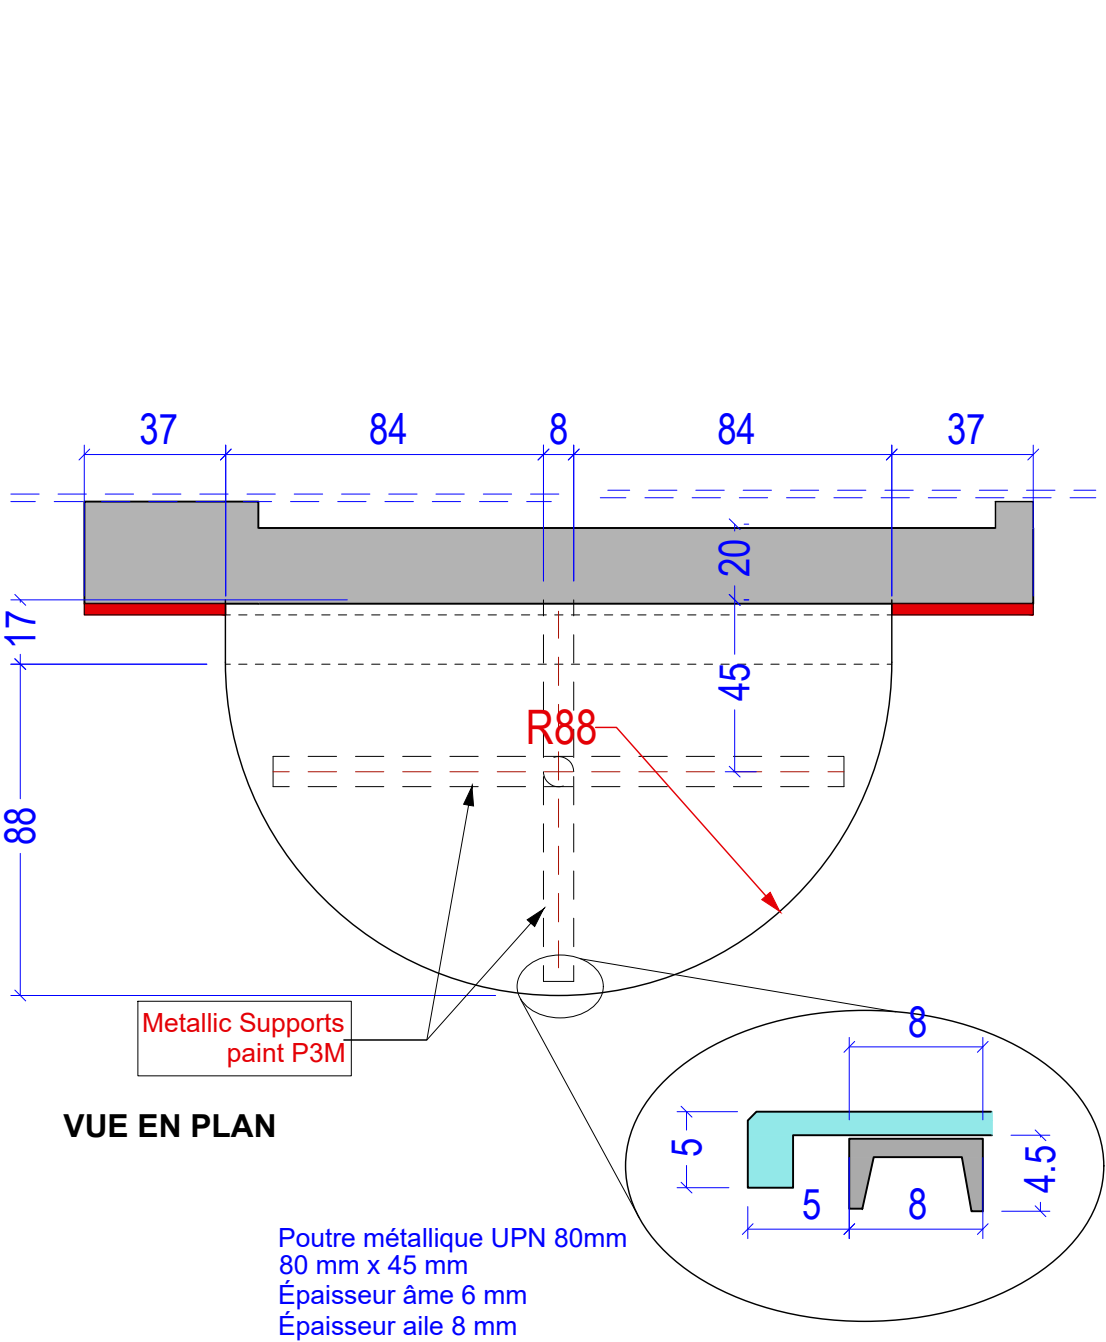

All joints welded and ground smooth. Tous les joints sont soudés et meulés lisses. Base of tube embedded in tile grout. Base du tube encastrée dans le coulis de carrelage

HUISSERIE	SOCLE METALLIQUE
VANTAIL	PANNEAU EN QUARTZ
QUINCAILLERIE	CHAVE + VISE D'ACCROCHAGE CHROMEES INVISIBLES EN INOX AU CHOIX DE L'ARCHITECTE
FINITION	SOCLE METALLIQUE EN PEINTURE COULEUR GRIS NOIR AU CHOIX DE L'ARCHITECTE

Constructor must submit shop drawings to architect for review showing actual dimensions verified in field

Le constructeur doit soumettre les dessins à l'architecte pour examen, indiquant les dimensions réelles vérifiées sur chantier.

MAITRE D'OUVRAGE: / OWNER
CONSUL GENERAL CASABLANCA

PROJET
RENOVATION CUISINE / KICHEN RENOVATION

PHASE
2 FEB 2026 -100% -FOR BID

Detaille menuiserie
Millwork Detail

ECHELLE/SCALE
1/20

A359

Brian Coffman - A359 sarl
Appt. 6, Imm 38 Av. Youssef Ben Tachfine, Rabat 10000
Tél : +212 671 159 257
E-mail : bcoffman@architecture359.ma
Web : www.architecture359.ma

REPERAGE

1-PL3
PLACARD EN BOIS
P 40 x L 1.16 x H 0.86

PLACARD EN BOIS

QUANTITE : 1





LOCALISATION :

CUISINE

N
O
M
E
N
C
L
A
T
U
R
E

&

D
E
T
A
I
L
S

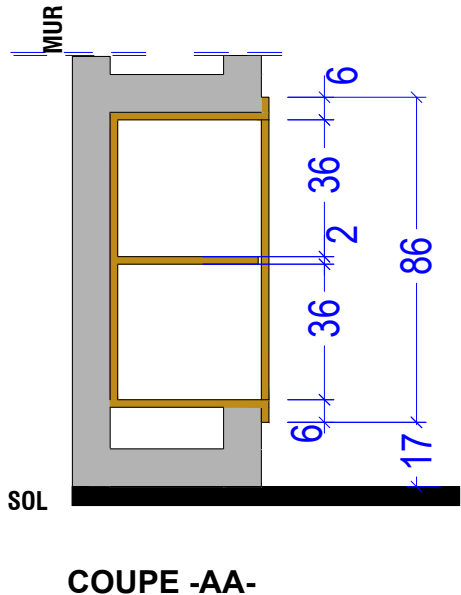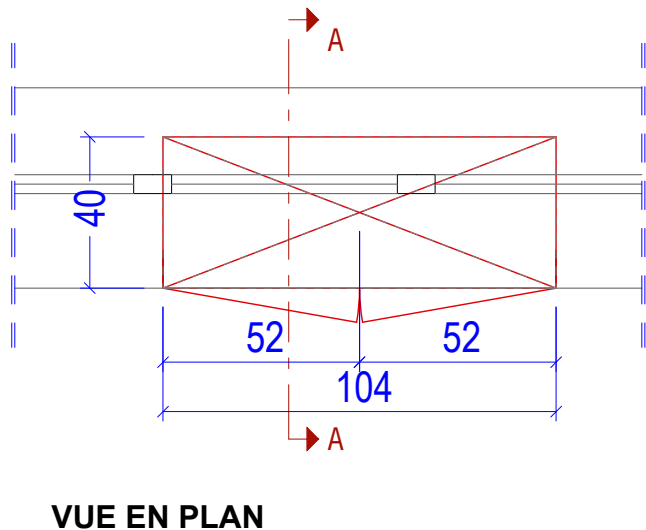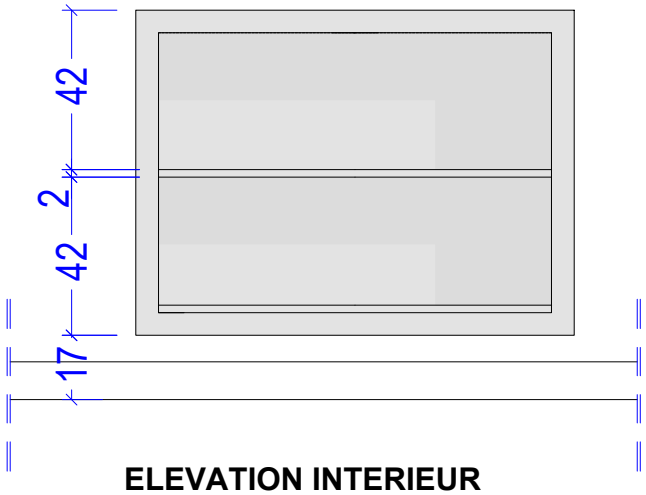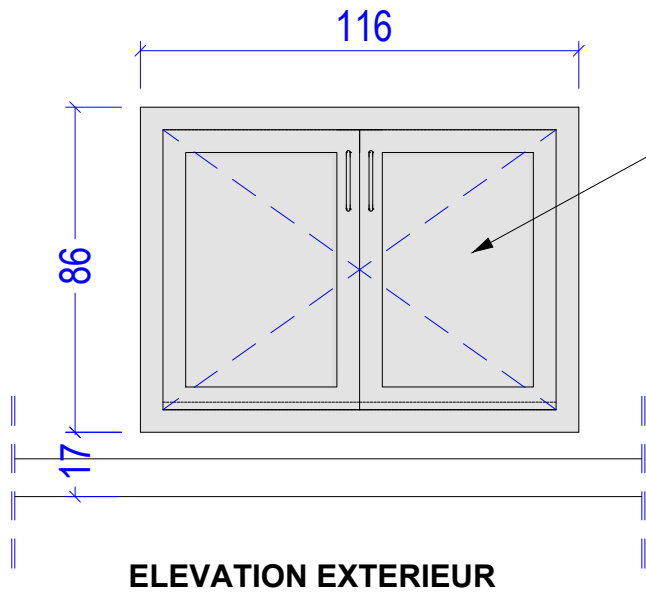

HUISSERIE
VANTAIL
QUINCAILLERIE
FINITION

CADRE EN BOIS ,
2 OUVRANT À LA FRANÇAISE
4 PAUMELLES ENCASTREES CHROMEES INVISIBLES EN INOX, 2 POIGNEES AU CHOIX DE L'ARCHITECTE
BOIS HETRE PEINTURE COULEUR GRIS NOIR AU CHOIX DE L'ARCHITECTE

Constructor must submit shop drawings to architect for review showing actual dimensions verified in field

Le constructeur doit soumettre les dessins à l'architecte pour examen, indiquant les dimensions réelles vérifiées sur chantier.

MAITRE D'OUVRAGE: / OWNER
CONSUL GENERAL CASABLANCA

PROJET
RENOVATION CUISINE / KICHEN RENOVATION

PHASE
2 FEB 2026 -100% -FOR BID

Detaille menuiserie
Millwork Detail

ECHELLE/SCALE
1/20

A359

Brian Coffman - A359 sarl
Appt. 6, Imm 38 Av. Youssef Ben Tachfine, Rabat 10000
Tél : +212 671 159 257
E-mail : bcoffman@architecture359.com
Web : www.architecture359.ma

REPERAGE

1-PL2

PLACARD EN BOIS
P 62 x L 2.30 x H 2.90


PLACARD EN BOIS

QUANTITE : 1

LOCALISATION :

CUISINE


N
O
M
E
N
C
L
A
T
U
R
E
&
D
E
T
A
I
L
S

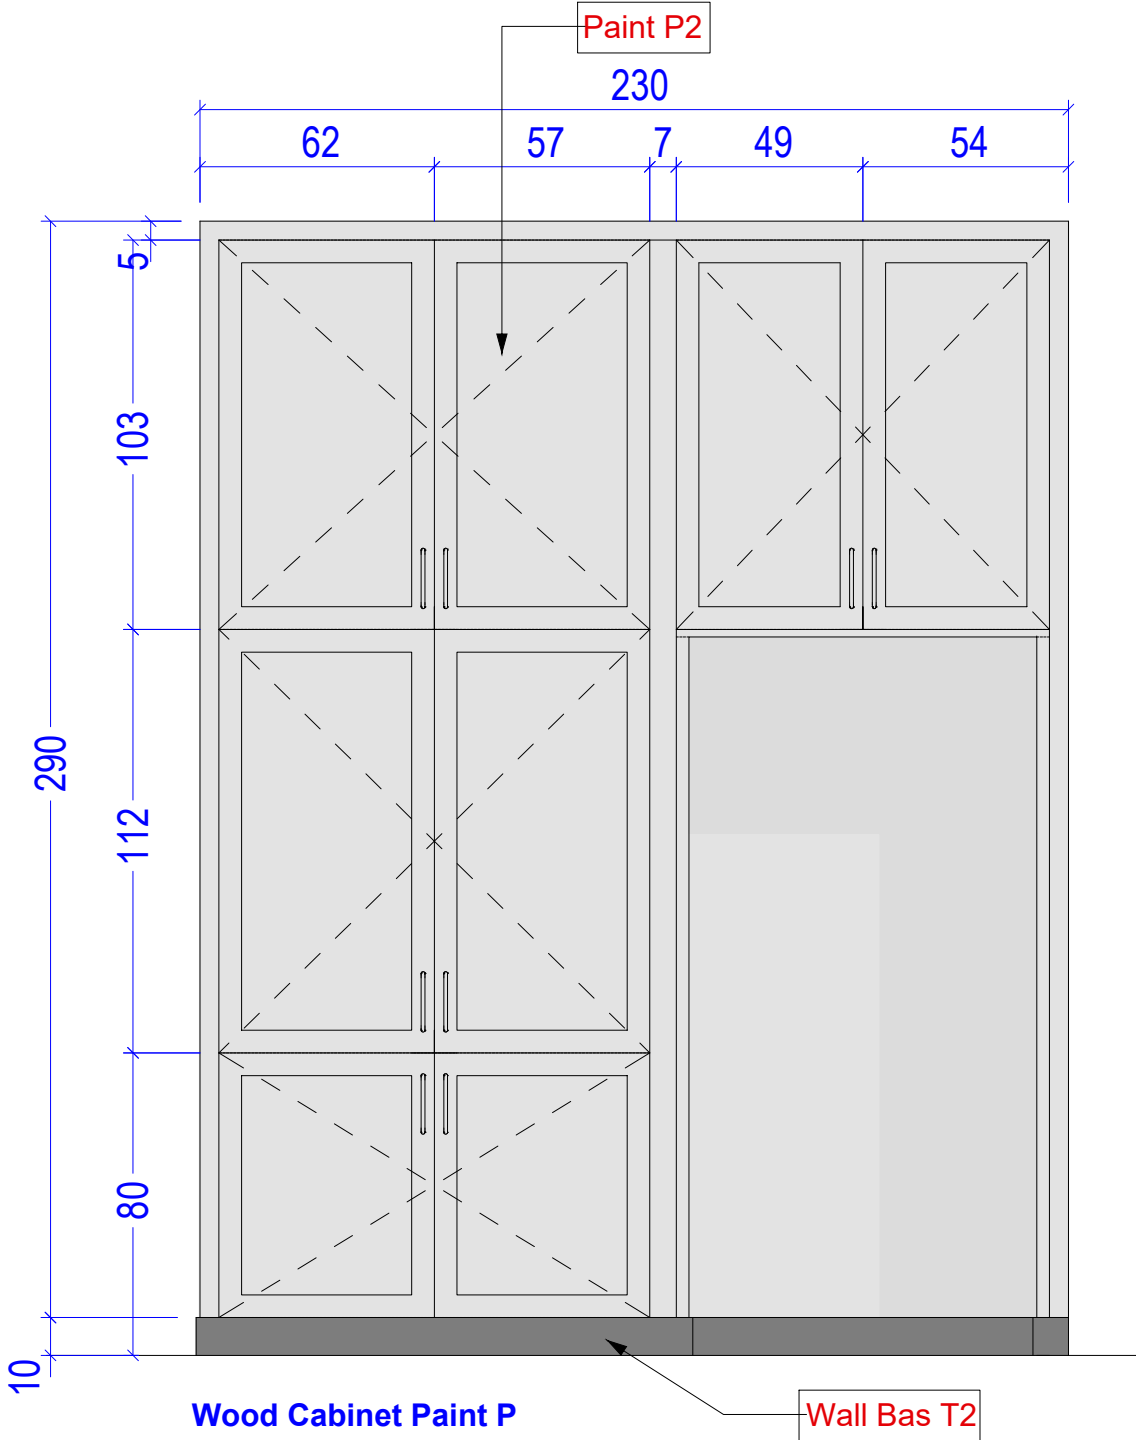

Wood Cabinet Paint P

Wall Bas T2

ELEVATION EXTERIEUR

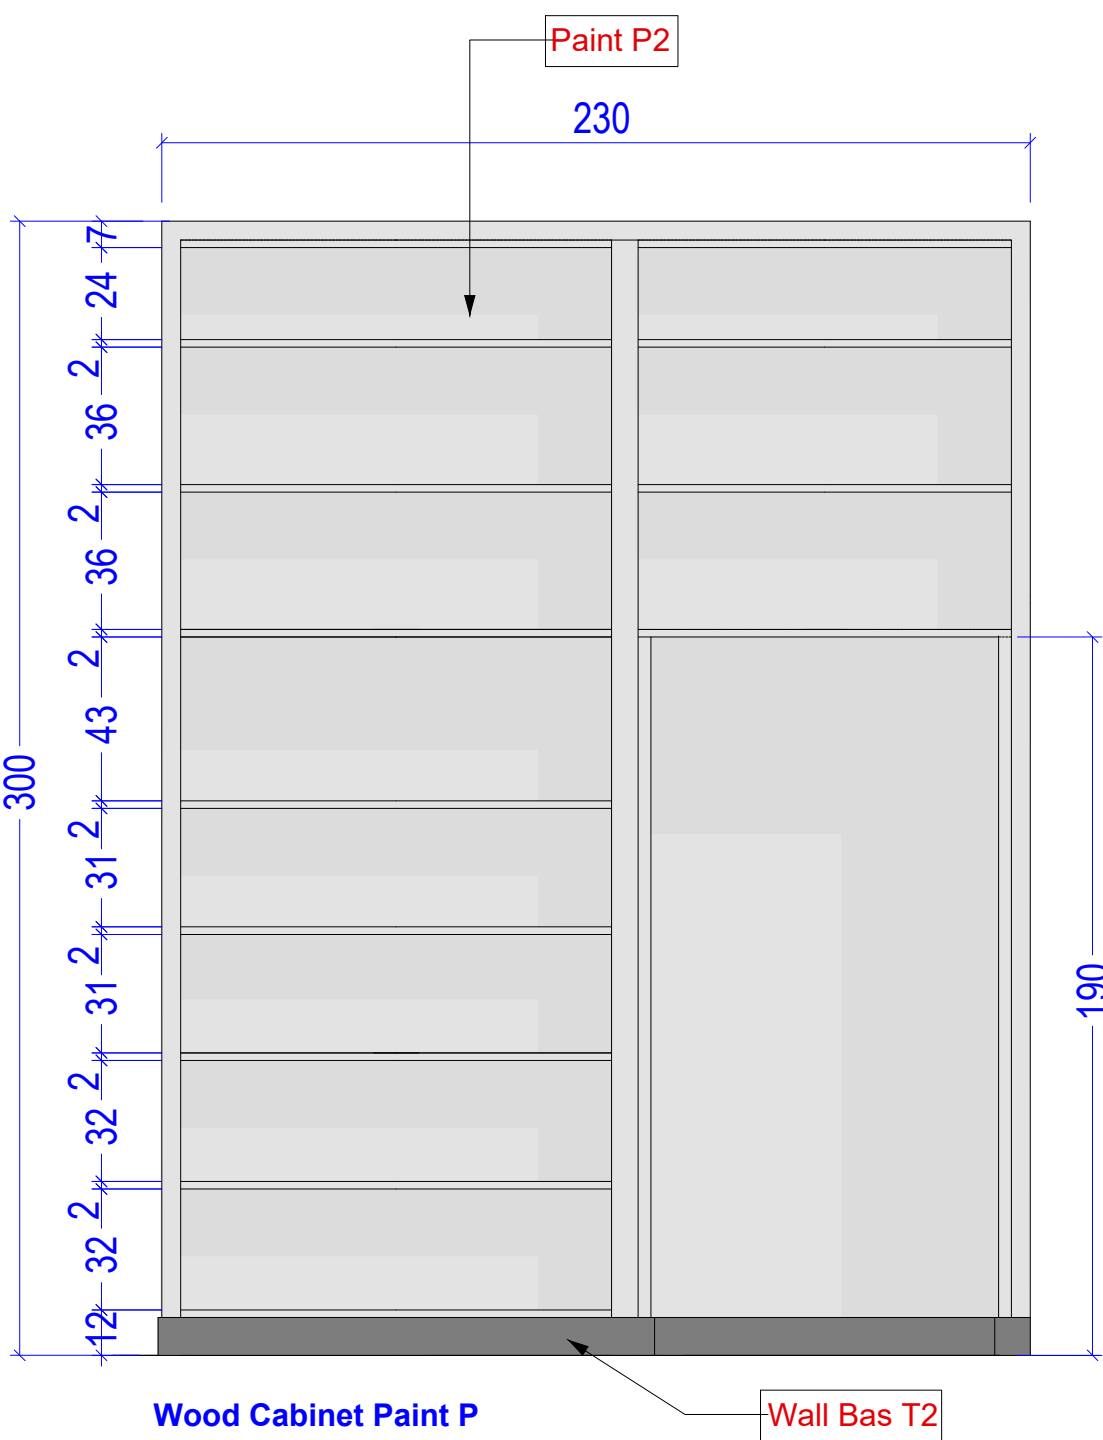

Wood Cabinet Paint P

Wall Bas T2

ELEVATION INTERIEUR

HUISSERIE

CADRE EN BOIS ,

VANTAIL

8 OUVRANT À LA FRANÇAISE

QUINCAILLERIE

16 PAUMELLES ENCASTREES CHROMEES INVISIBLES EN INOX, 8 POIGNEES AU CHOIX DE L'ARCHITECTE

FINITION

BOIS HETRE PEINTURE COULEUR GRIS NOIR AU CHOIX DE L'ARCHITECTE

Constructor must submit shop drawings to architect for review
showing actual dimensions verified in field

Le constructeur doit soumettre les dessins à l'architecte pour
examen, indiquant les dimensions réelles vérifiées sur chantier.

MAITRE D'OUVRAGE: / OWNER
CONSUL GENERAL CASABLANCA

PROJET
RENOVATION CUISINE / KICHEN RENOVATION

PHASE
2 FEB 2026 -100% -FOR BID

Detaille menuiserie
Millwork Detail

ECHELLE/SCALE
1/20

A359

Brian Coffman - A359 sarl
Appt. 6, Imm 38 Av. Youssef Ben Tachfine, Rabat 10000
Tél : +212 671 159 257
E-mail : bcoffman@architecture359.com
Web : www.architecture359.ma

REPERAGE

1-P.T 1

PLAN TRAVAIL
0,65 X 2,95 X 0,90




PLAN TRAVAIL DE CUISINE AVEC QUARTZ

QUANTITE : 1

LOCALISATION :

CUISINE

N
O
M
E
N
C
L
A
T
U
R
E
&
D
E
T
A
I
L
S

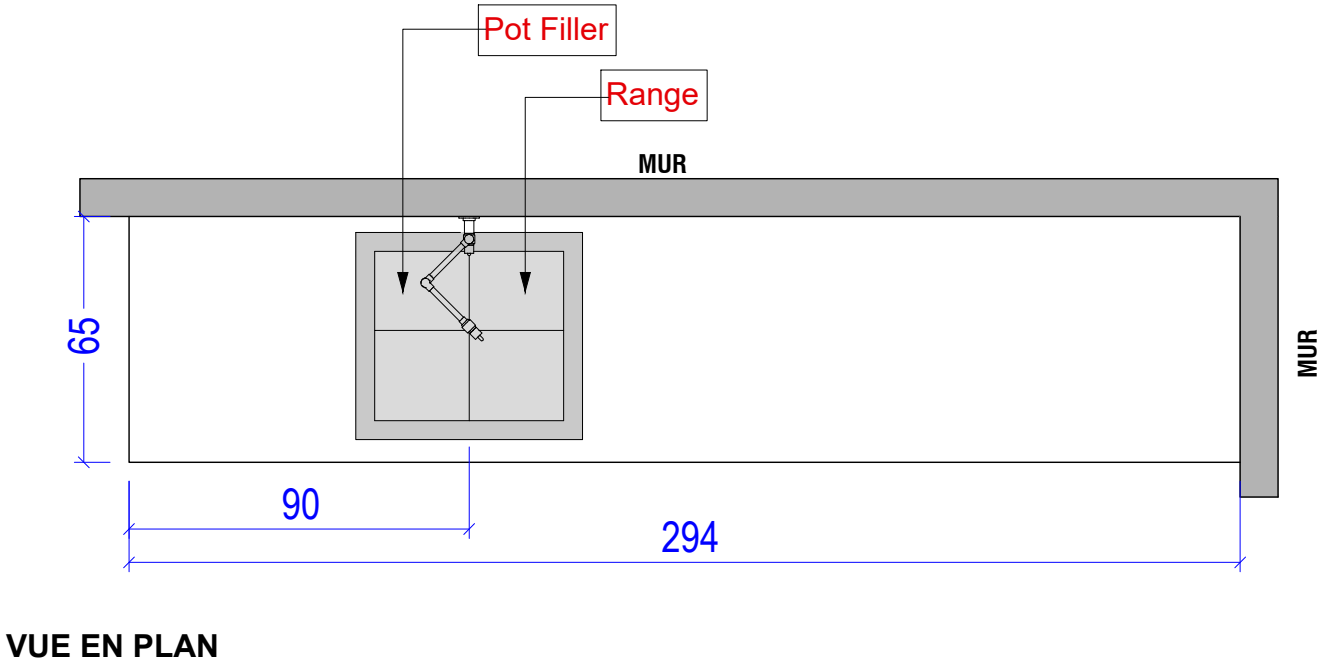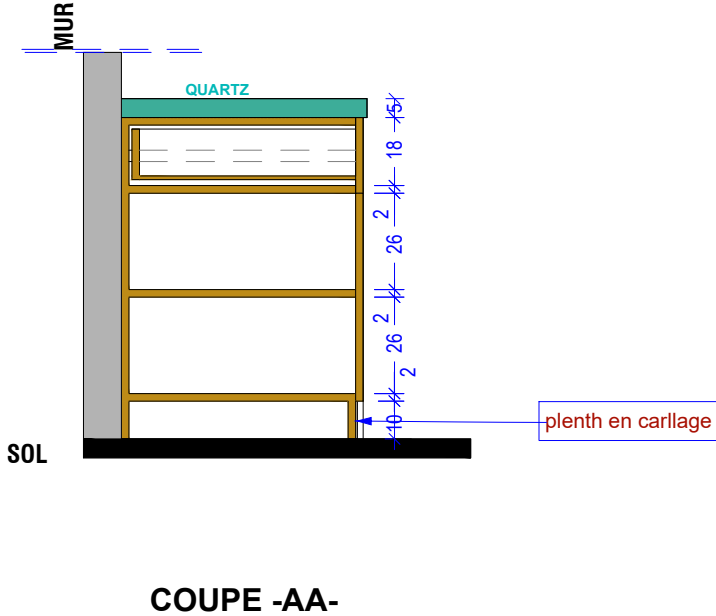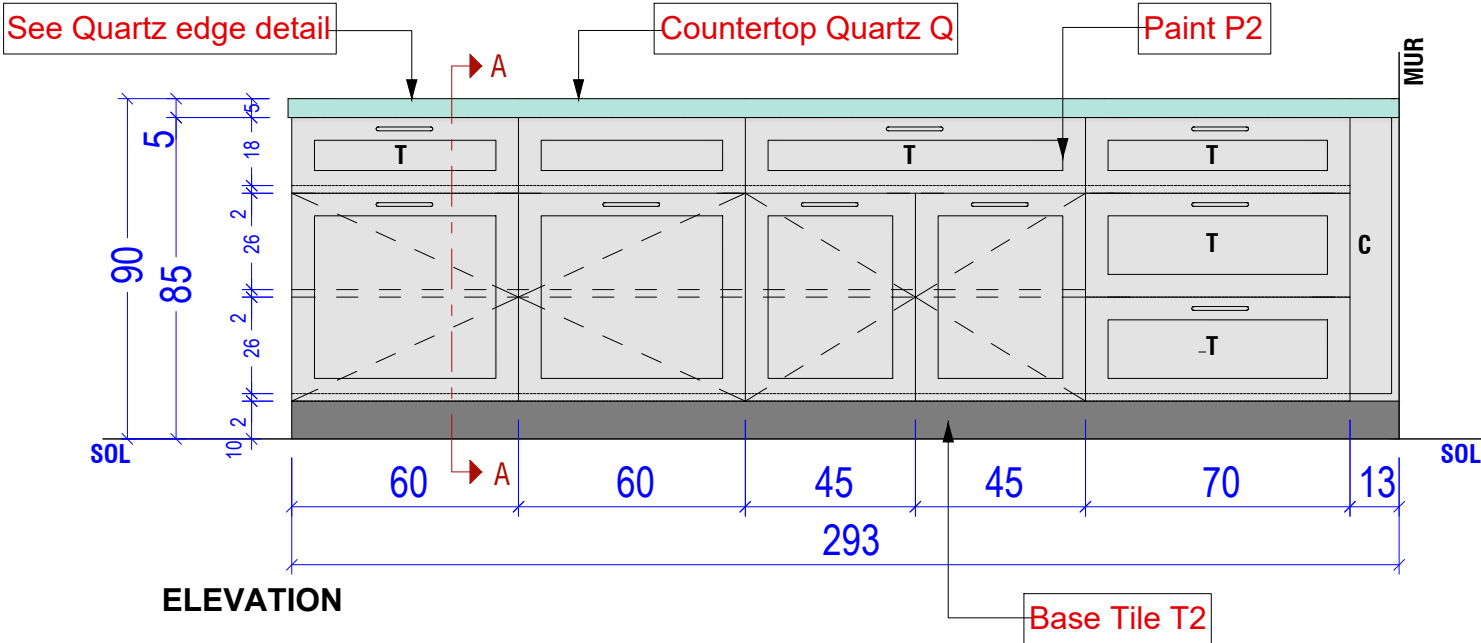

HUISSERIE

CADRE EN BOIS

VANTAIL

4 OUVRANT A LA FRANCAISE + 5 TIROIRS

QUINCAILLERIE

8 PAUMELLES 140 x 80 CHROMEES INVISIBLES EN INOX, 10 RAIL TIROIR 9 POIGNEES EN INOX, AU CHOIX DE L'ARCHITECTE

FINITION

BOIS HETRE PEINTURE COULEUR AU CHOIX DE L'ARCHITECTE

Constructor must submit shop drawings to architect for review showing actual dimensions verified in field

Le constructeur doit soumettre les dessins à l'architecte pour examen, indiquant les dimensions réelles vérifiées sur chantier.

MAITRE D'OUVRAGE: / OWNER
CONSUL GENERAL CASABLANCA

PROJET
RENOVATION CUISINE / KICHEN RENOVATION

PHASE
2 FEB 2026 -100% -FOR BID

Detaille menuiserie
Millwork Detail

ECHELLE/SCALE
1/20

A359

Brian Coffman - A359 sarl
Appt. 6, Imm 38 Av. Youssef Ben Tachfine, Rabat 10000
Tél : +212 671 159 257
E-mail : bcoffman@architecture359.com
Web : www.architecture359.ma

REPERAGE

1-PL.H 1

PLACARD HAUT
0,60 X 1,66 X 0,48

PLACARD HAUT + ETAGERE

QUANTITE : 1




LOCALISATION :

CUISINE

N
O
M
E
N
C
L
A
T
U
R
E

&

D
E
T
A
I
L
S

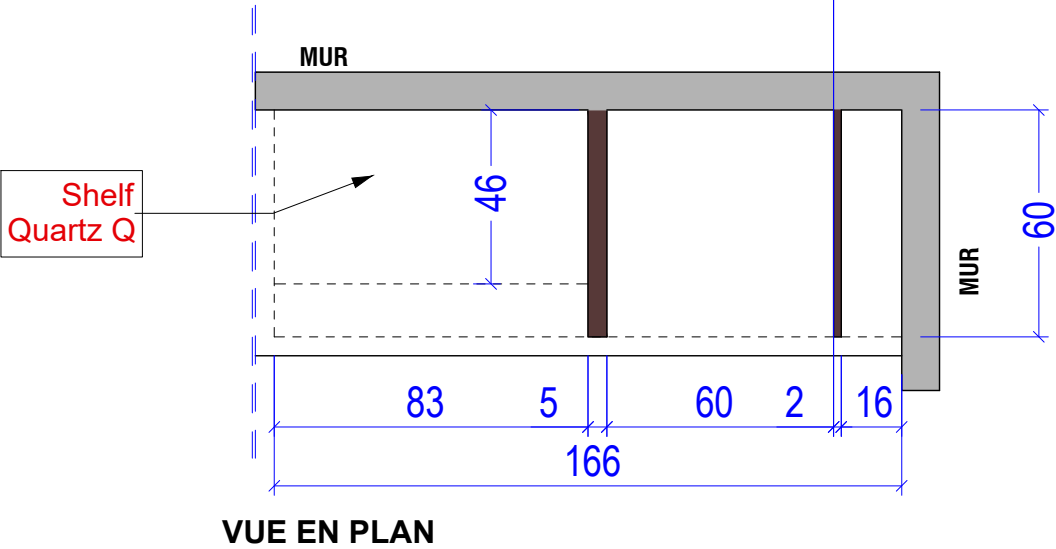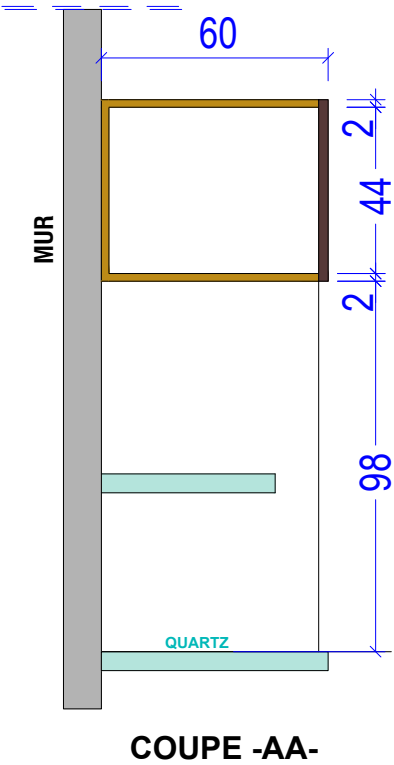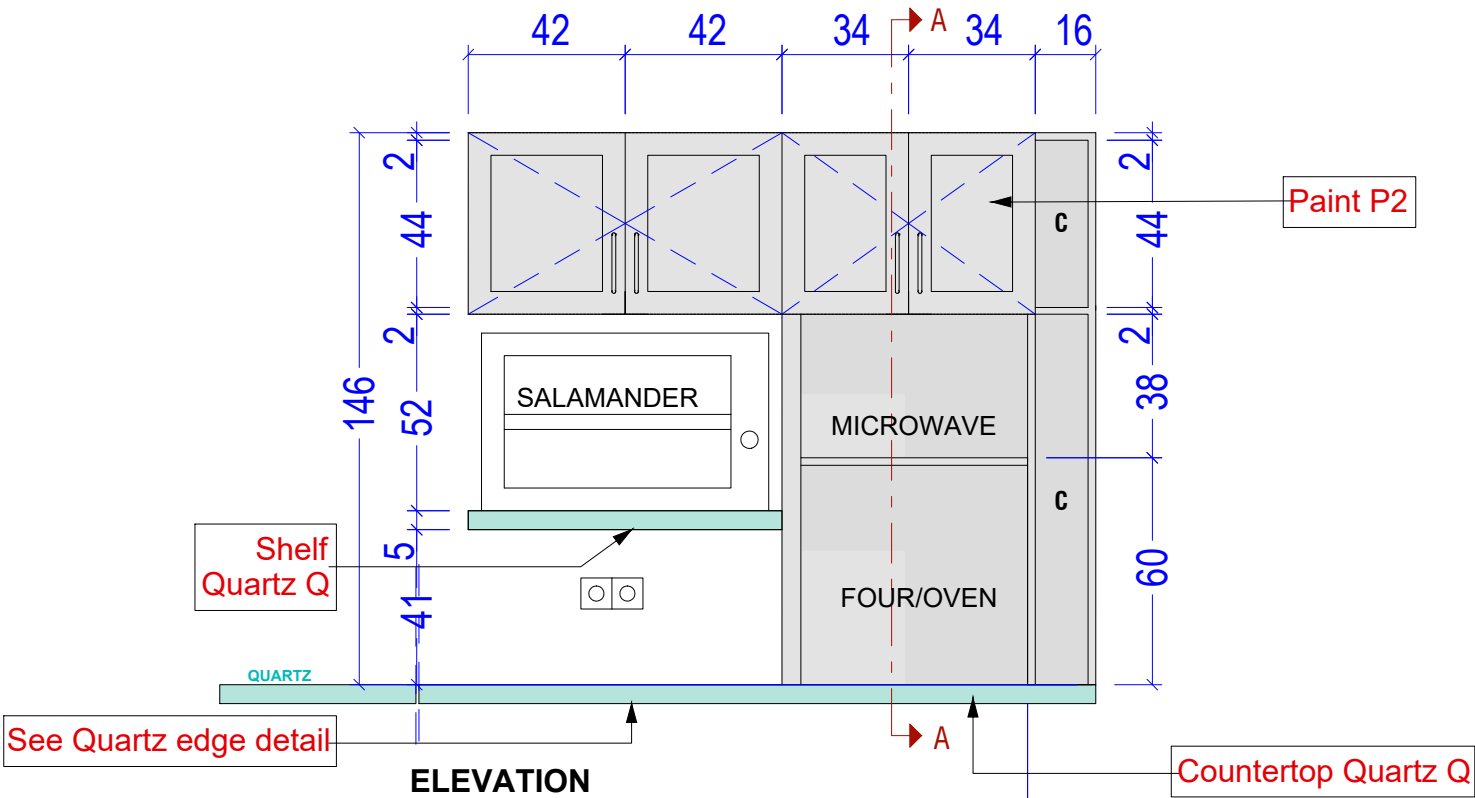

HUISSERIE

CADRE EN BOIS

VANTAIL

4 OUVRANT A LA FRANCAISE

QUINCAILLERIE

8 PAUMELLES 140 x 80 CHROMEES INVISIBLES EN INOX, 4 POIGNEES EN INOX, AU CHOIX DE L'ARCHITECTE

FINITION

BOIS HETRE PEINTURE COULEUR AU CHOIX DE L'ARCHITECTE

Constructor must submit shop drawings to architect for review showing actual dimensions verified in field

Le constructeur doit soumettre les dessins à l'architecte pour examen, indiquant les dimensions réelles vérifiées sur chantier.

MAITRE D'OUVRAGE: / OWNER
CONSUL GENERAL CASABLANCA

PROJET
RENOVATION CUISINE / KICHEN RENOVATION

PHASE
2 FEB 2026 -100% -FOR BID

Detaille menuiserie
Millwork Detail

ECHELLE/SCALE
1/20

A359

Brian Coffman - A359 sarl
Appt. 6, Imm 38 Av. Youssef Ben Tachfine, Rabat 10000
Tél : +212 671 159 257
E-mail : bcoffman@architecture359.com
Web : www.architecture359.ma

REPERAGE

1-P.T 2

PLAN TRAVAIL
0,65 X 2,67 X 0,90

PLAN TRAVAIL DE CUISINE AVEC QUARTZ



QUANTITE : 1

LOCALISATION : CUISINE



N
O
M
E
N
C
L
A
T
U
R
E

&

D
E
T
A
I
L
S

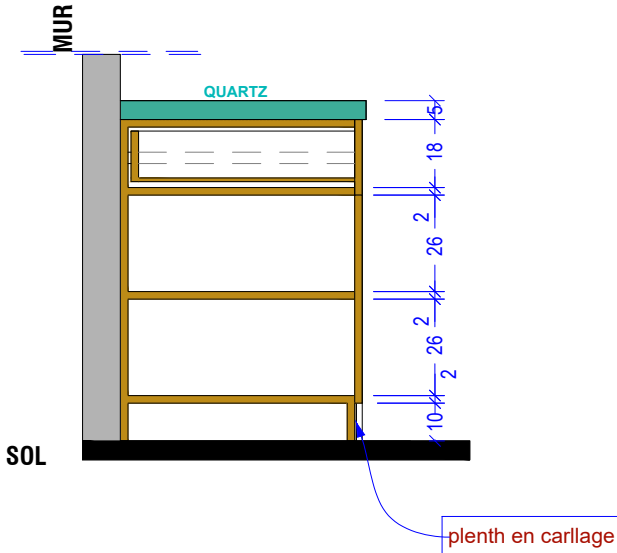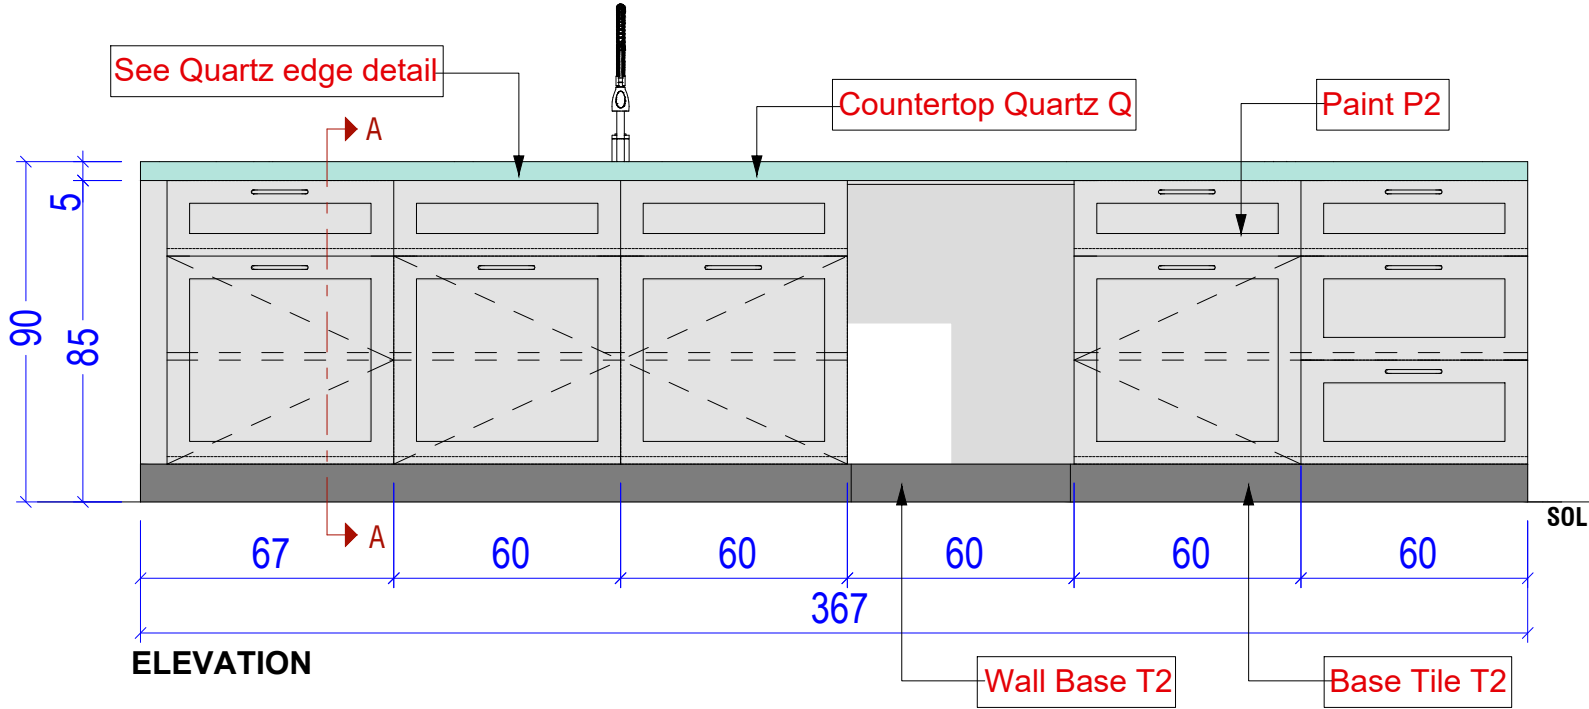

COUPE -AA-

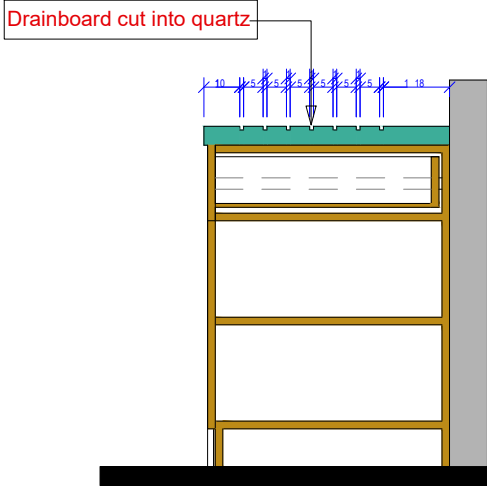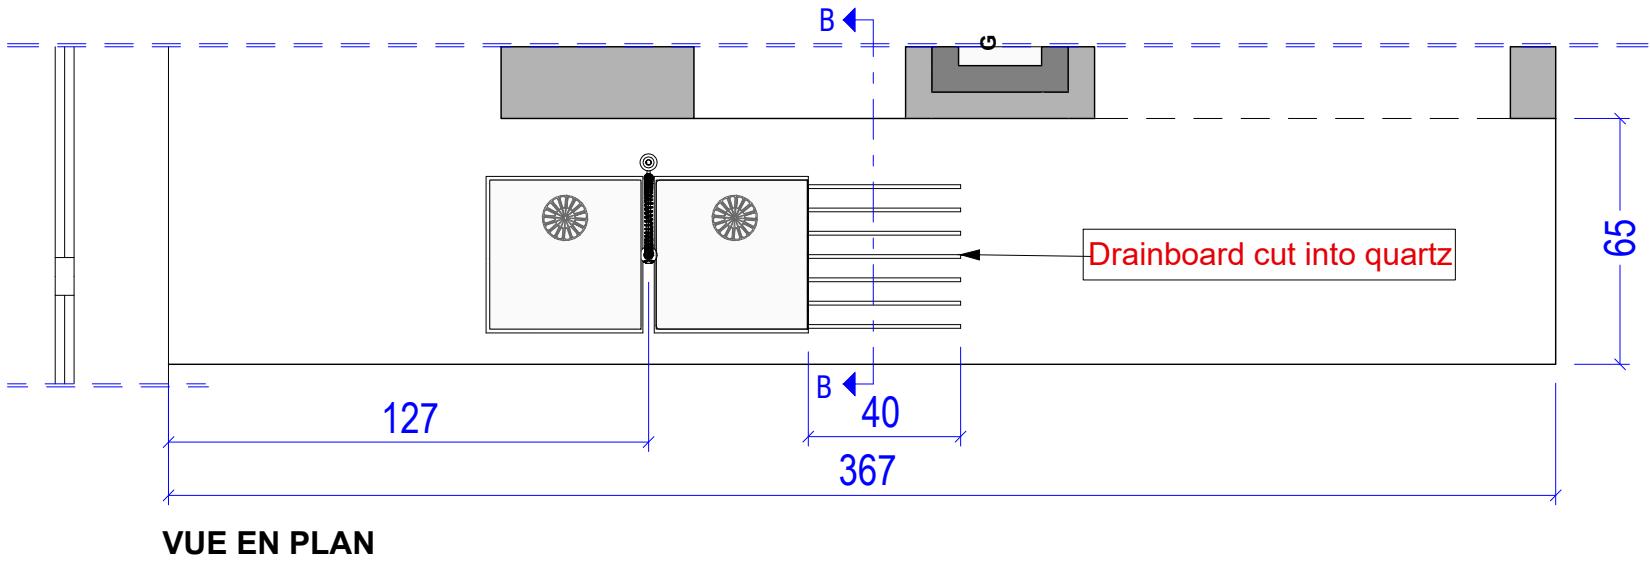

COUPE -BB-

HUISSERIE	CADRE EN BOIS
VANTAIL	4 OUVRANT A LA FRANCAISE + 5 TIROIRS
QUINCAILLERIE	8 PAUMELLES 140 x 80 CHROMEES INVISIBLES EN INOX, 10 RAIL TIROIR 9 POIGNEES EN INOX, AU CHOIX DE L'ARCHITECTE
FINITION	BOIS HETRE PEINTURE COULEUR AU CHOIX DE L'ARCHITECTE

Constructor must submit shop drawings to architect for review showing actual dimensions verified in field

Le constructeur doit soumettre les dessins à l'architecte pour examen, indiquant les dimensions réelles vérifiées sur chantier.

MAITRE D'OUVRAGE: / OWNER
CONSUL GENERAL CASABLANCA

PROJET
RENOVATION CUISINE / KICHEN RENOVATION

PHASE
2 FEB 2026 -100% -FOR BID

Detaille menuiserie
Millwork Detail

ECHELLE/SCALE
1/20

A359

Brian Coffman - A359 sarl
Appt. 6, Imm 38 Av. Youssef Ben Tachfine, Rabat 10000
Tél : +212 671 159 257
E-mail : bcoffman@architecture359.com
Web : www.architecture359.ma

REPERAGE

1-PL.H 2

PLAN TRAVAIL
0,60 X 2,55 X 0,70


PLACARD HAUT + ETAGERE

LOCALISATION :


CUISINE

QUANTITE : 1


N
O
M
E
N
C
L
A
T
U
R
E
&
D
E
T
A
I
L
S

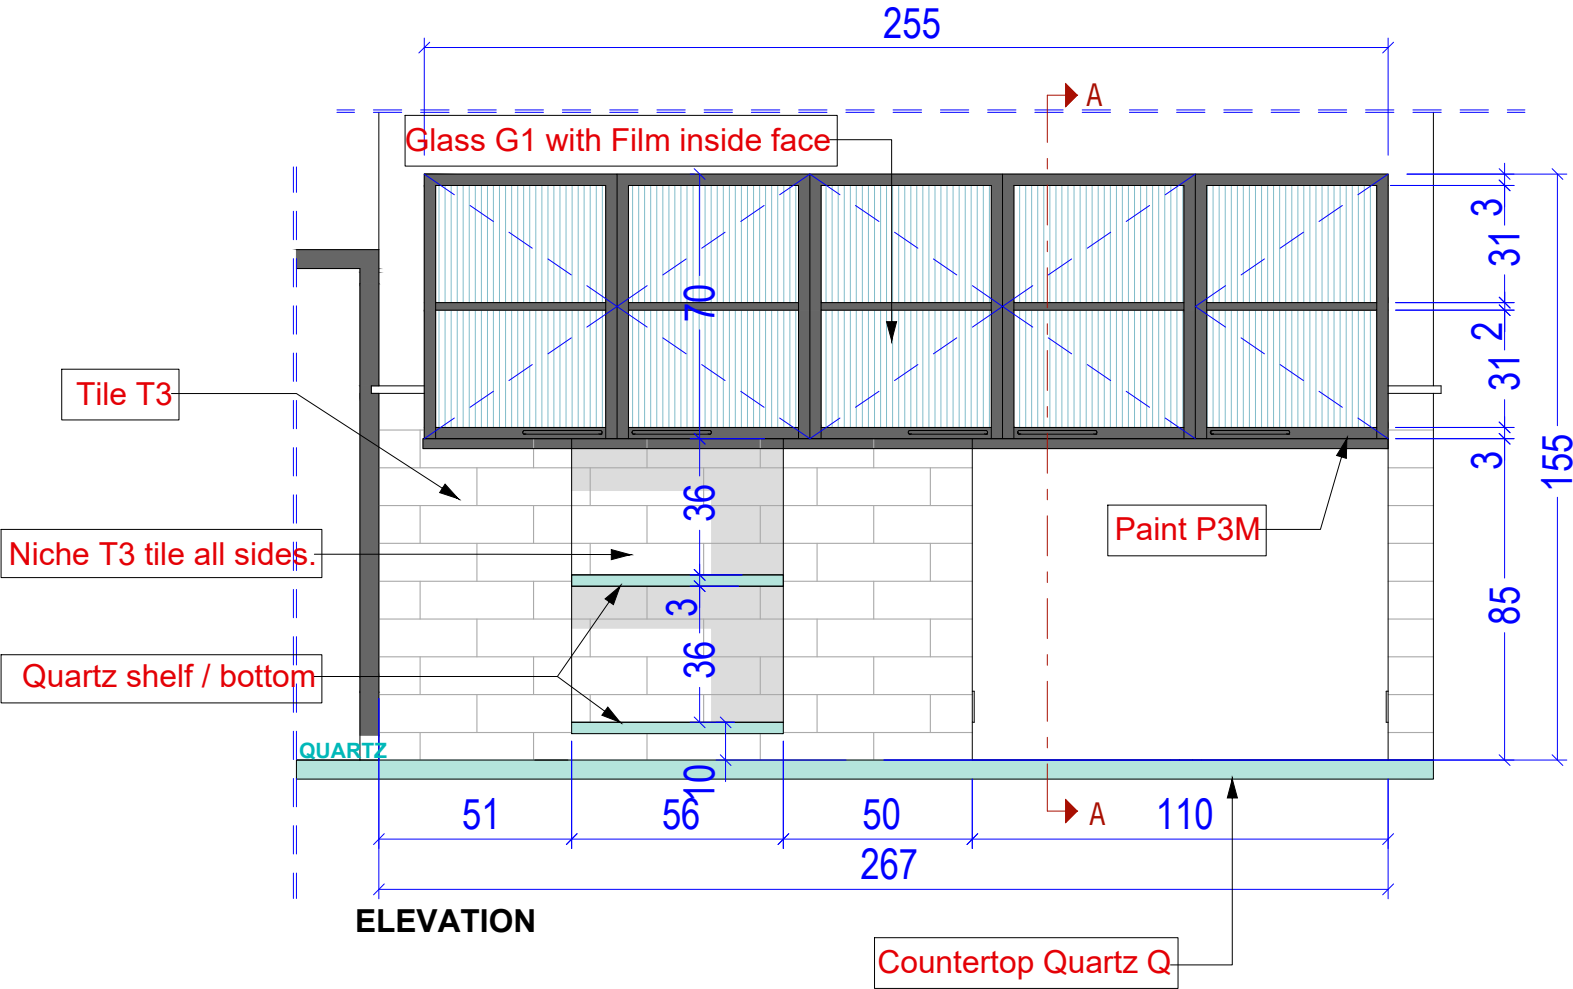

ELEVATION

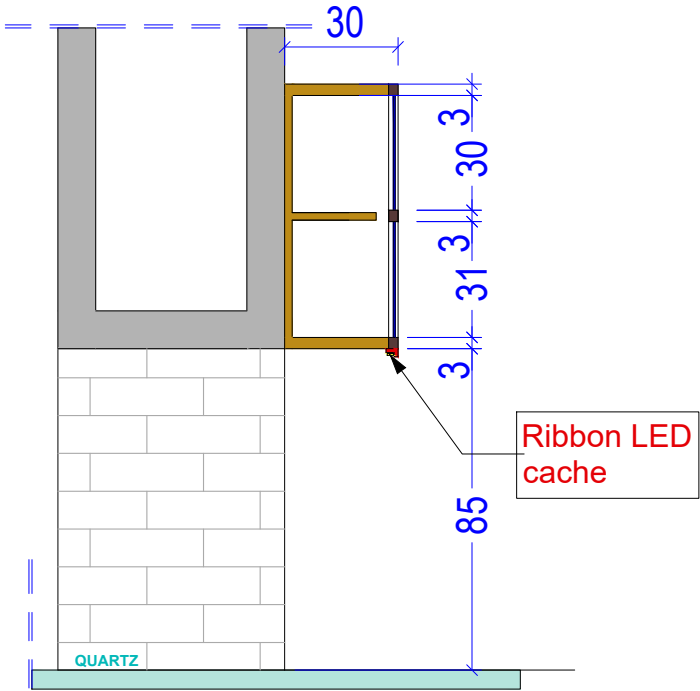

COUPE -AA-

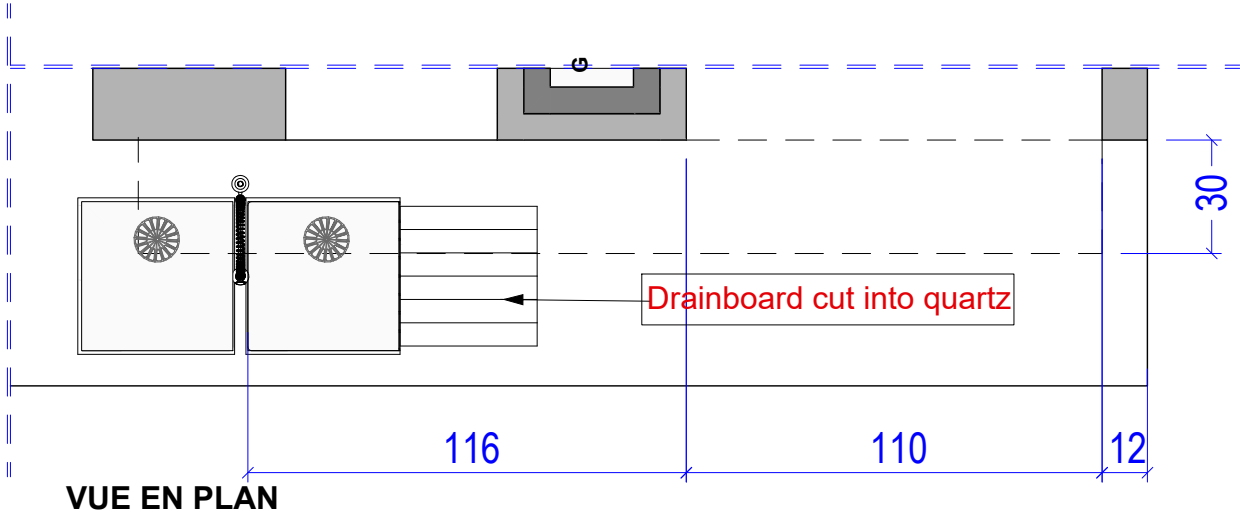

VUE EN PLAN

HUISSERIE

CADRE EN BOIS PORTE METALLIQUE VITREE SABLEE

VANTAIL

5 OUVRANT A LA FRANCAISE

QUINCAILLERIE

10 PAUMELLES 140 x 80 CHROMEES INVISIBLES EN INOX, 5 POIGNEES EN INOX, AU CHOIX DE L'ARCHITECTE

FINITION

BOIS HETRE PEINTURE COULEUR GRIS NOIR AU CHOIX DE L'ARCHITECTE

Constructor must submit shop drawings to architect for review showing actual dimensions verified in field

Le constructeur doit soumettre les dessins à l'architecte pour examen, indiquant les dimensions réelles vérifiées sur chantier.

MAITRE D'OUVRAGE: / OWNER
CONSUL GENERAL CASABLANCA

PROJET
RENOVATION CUISINE / KITCHEN RENOVATION

PHASE
2 FEB 2026 -100% -FOR BID

Detaille menuiserie
Millwork Detail

ECHELLE/SCALE
1/20

A359

Brian Coffman - A359 sarl
Appt. 6, Imm 38 Av. Youssef Ben Tachfine, Rabat 10000
Tél : +212 671 159 257
E-mail : bcoffman@architecture359.com
Web : www.architecture359.ma

REPERAGE

1-P.T 3

PLAN TRAVAIL
0,65 X 3,90 X 0,90

PLAN TRAVAIL DE CUISINE AVEC QUARTZ

QUANTITE : 1



LOCALISATION :

CUISINE



N
O
M
E
N
C
L
A
T
U
R
E

&

D
E
T
A
I
L
S

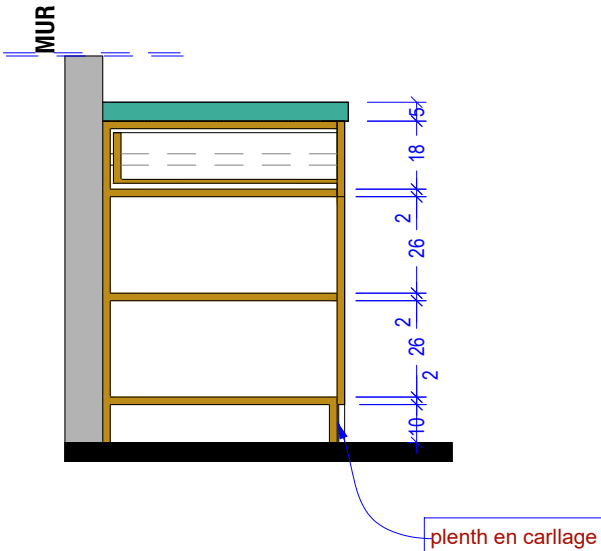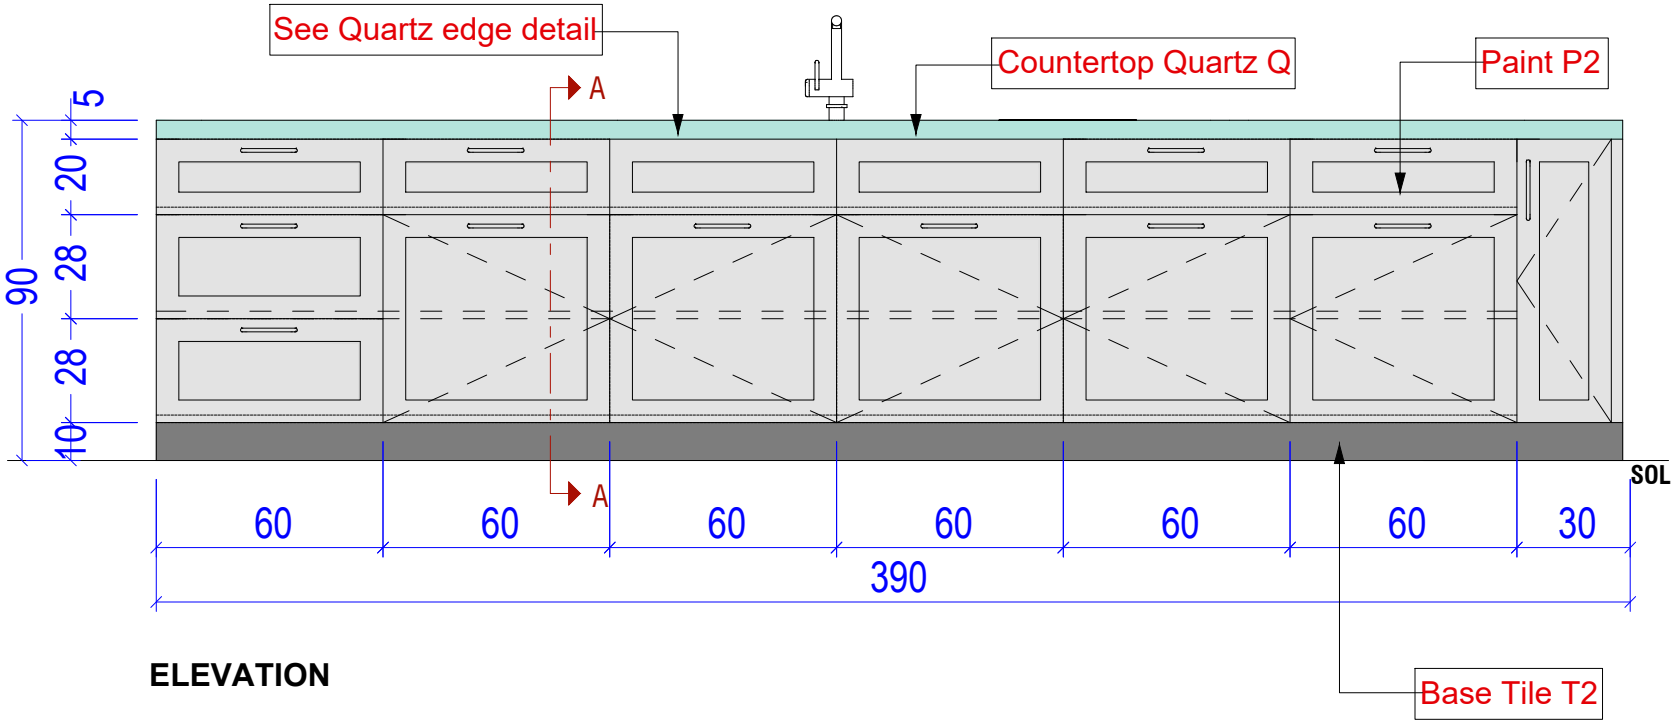

COUPE -AA-

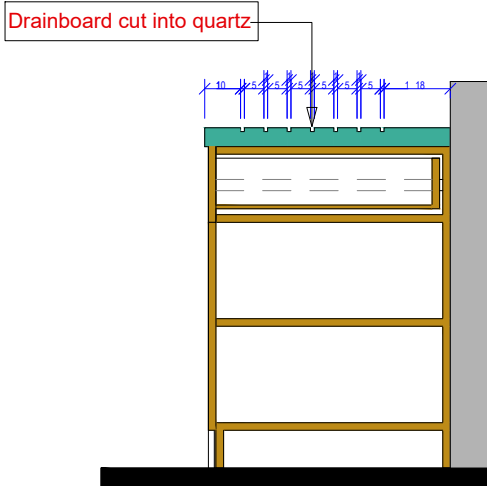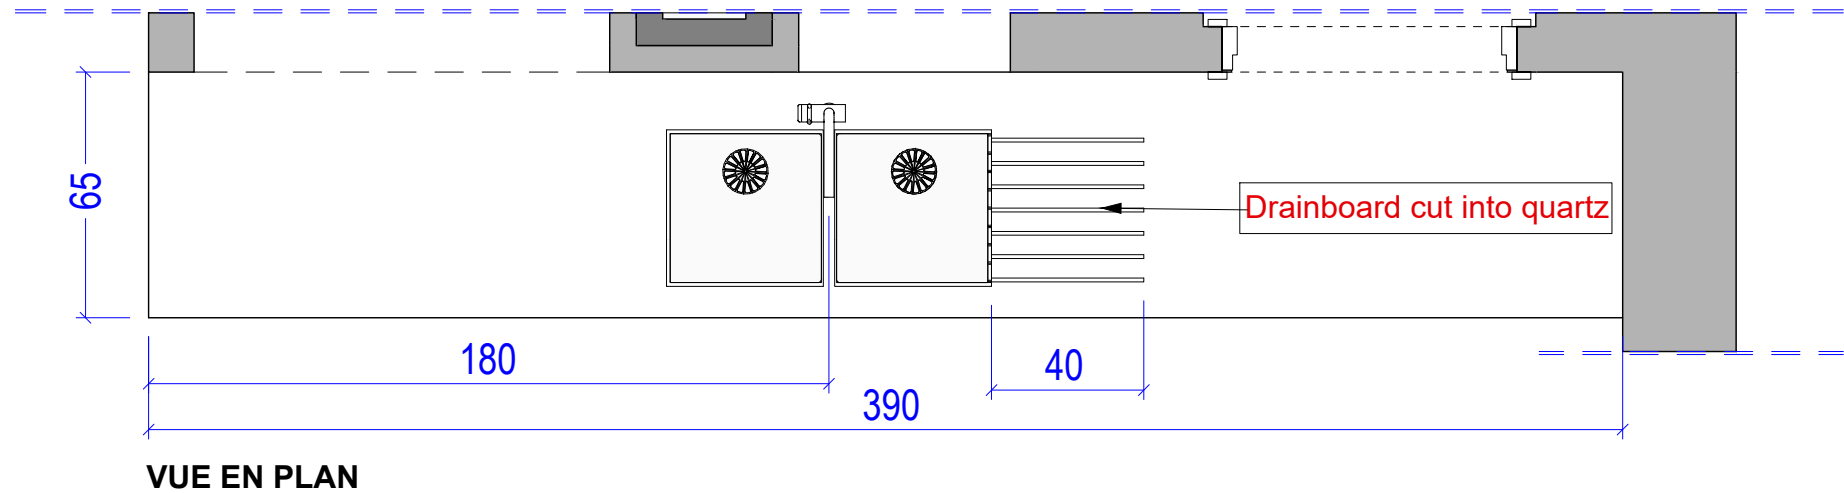

COUPE -BB-

HUISSERIE

CADRE EN BOIS

VANTAIL

6 OUVRANT A LA FRANCAISE + 6 TIROIRS

QUINCAILLERIE

12 PAUMELLES 140 x 80 CHROMEES INVISIBLES EN INOX, 12 RAIL TIROIR 9 POIGNEES EN INOX, AU CHOIX DE L'ARCHITECTE

FINITION

BOIS HETRE PEINTURE COULEUR AU CHOIX DE L'ARCHITECTE

Constructor must submit shop drawings to architect for review showing actual dimensions verified in field

Le constructeur doit soumettre les dessins à l'architecte pour examen, indiquant les dimensions réelles vérifiées sur chantier.

MAITRE D'OUVRAGE: / OWNER
CONSUL GENERAL CASABLANCA

PROJET
RENOVATION CUISINE / KICHEN RENOVATION

PHASE
2 FEB 2026 -100% -FOR BID

Detaille menuiserie
Millwork Detail

ECHELLE/SCALE
1/20

A359

Brian Coffman - A359 sarlau
Appt. 6, Imm 38 Av. Youssef Ben Tachfine, Rabat 10000
Tél : +212 671 159 257
E-mail : bcoffman@architecture359.com
Web : www.architecture359.ma

REPERAGE

1-PL.H 3

PLAN TRAVAIL
0,60 X 2,55 X 0,70

PLACARD HAUT + ETAGERE

QUANTITE : 1


LOCALISATION :

CUISINE


N
O
M
E
N
C
L
A
T
U
R
E

&


D
E
T
A
I
L
S

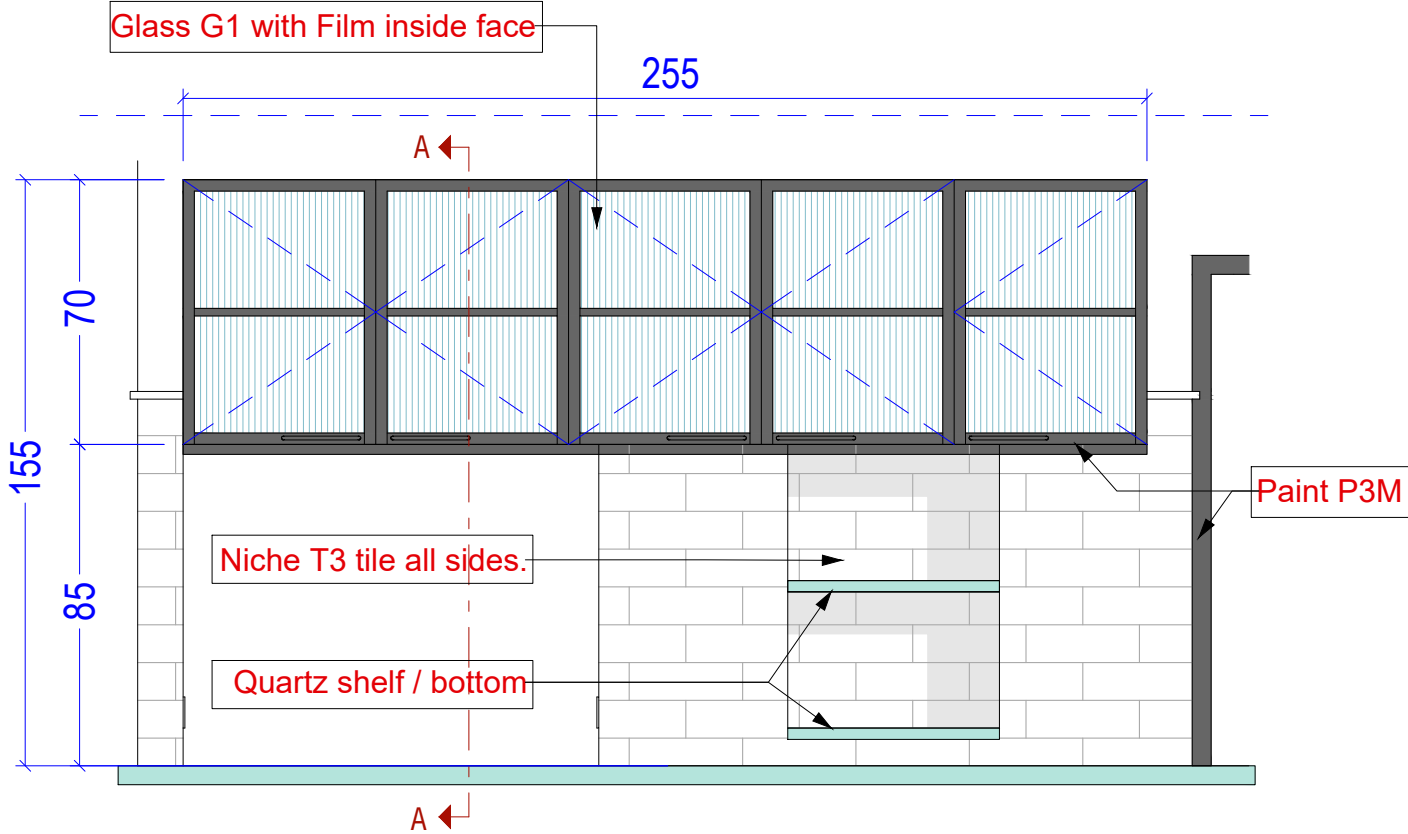

ELEVATION

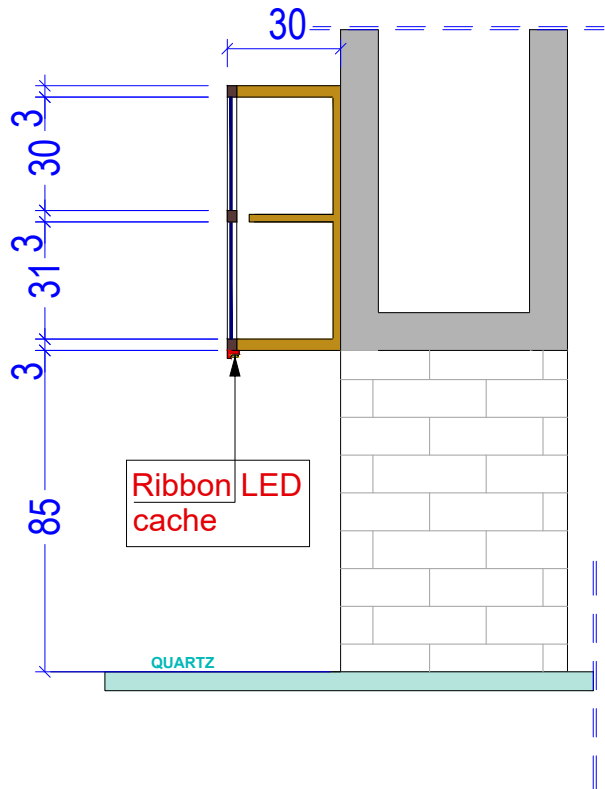

COUPE -AA-

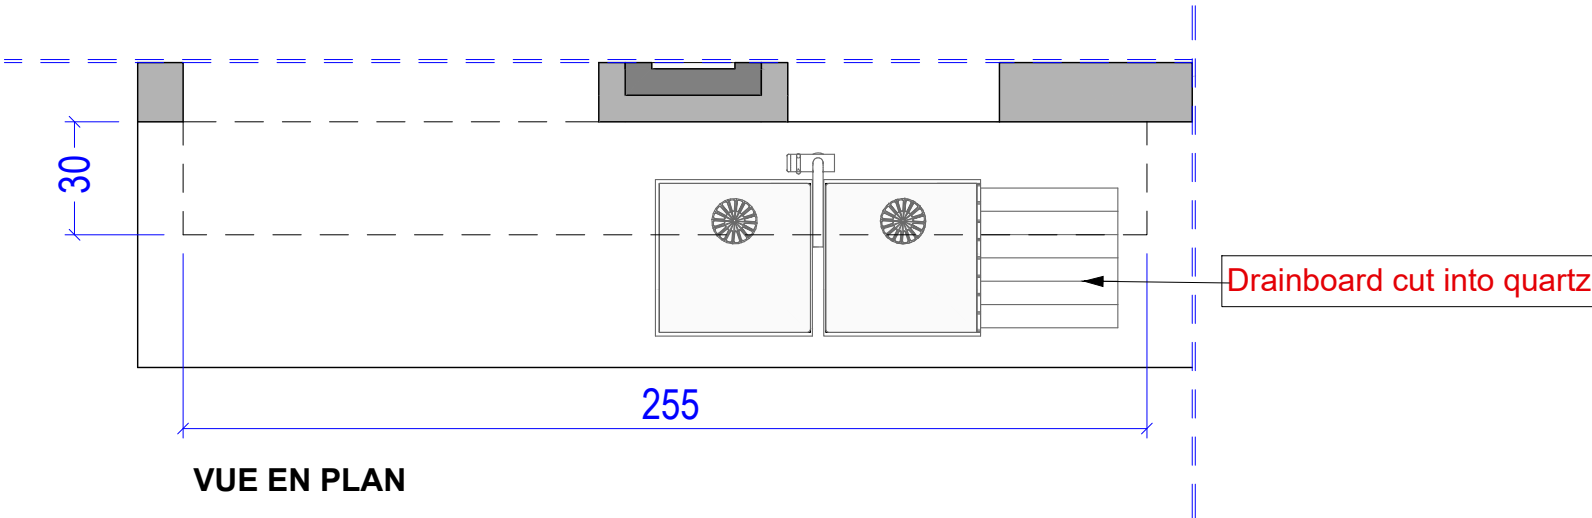

VUE EN PLAN

HUISSERIE

CADRE EN BOIS PORTE METALLIQUE VITREE SABLEE

VANTAIL

5 OUVRANT A LA FRANCAISE

QUINCAILLERIE

10 PAUMELLES 140 x 80 CHROMEES INVISIBLES EN INOX, 5 POIGNEES EN INOX, AU CHOIX DE L'ARCHITECTE

FINITION

BOIS HETRE PEINTURE COULEUR GRIS NOIR AU CHOIX DE L'ARCHITECTE

Constructor must submit shop drawings to architect for review showing actual dimensions verified in field

Le constructeur doit soumettre les dessins à l'architecte pour examen, indiquant les dimensions réelles vérifiées sur chantier.

MAITRE D'OUVRAGE: / OWNER
CONSUL GENERAL CASABLANCA

PROJET
RENOVATION CUISINE / KICHEN RENOVATION

PHASE
2 FEB 2026 -100% -FOR BID

Detaille menuiserie
Millwork Detail

ECHELLE/SCALE
1/20

A359

Brian Coffman - A359 sarl
Appt. 6, Imm 38 Av. Youssef Ben Tachfine, Rabat 10000
Tél : +212 671 159 257
E-mail : bcoffman@architecture359.com
Web : www.architecture359.ma

ROYAUME DU MAROC
WILAYA DE DE LA REGION
CASABLANCA - SETTAT

MAITRE D'OUVRAGE :

PROJET :
CONSUL GENERAL RESIDENCE - CASABLANCA - KITCHEN RENOVATION

ARCHITECTE :



Bureau de Contrôle :

Entreprise :

Révision	Date	Modifications - Observations	Dessiné	Vérifié	Approuvé
A	10-2024	1ère EMISSION			
B	06 JAN 2026	90% REVISION			
C	02 FEB 2026	100% FOR BID			

AO :
LOT PLOMBERIE SANITAIRE
REZ DE CHAUSSÉE, SOUS SOL
EVACUATION EAU USEE

Client	Plan N° 01	PLB	Indice A
AFFAIRE N°	DESSINE PAR	VERIFIE PAR	

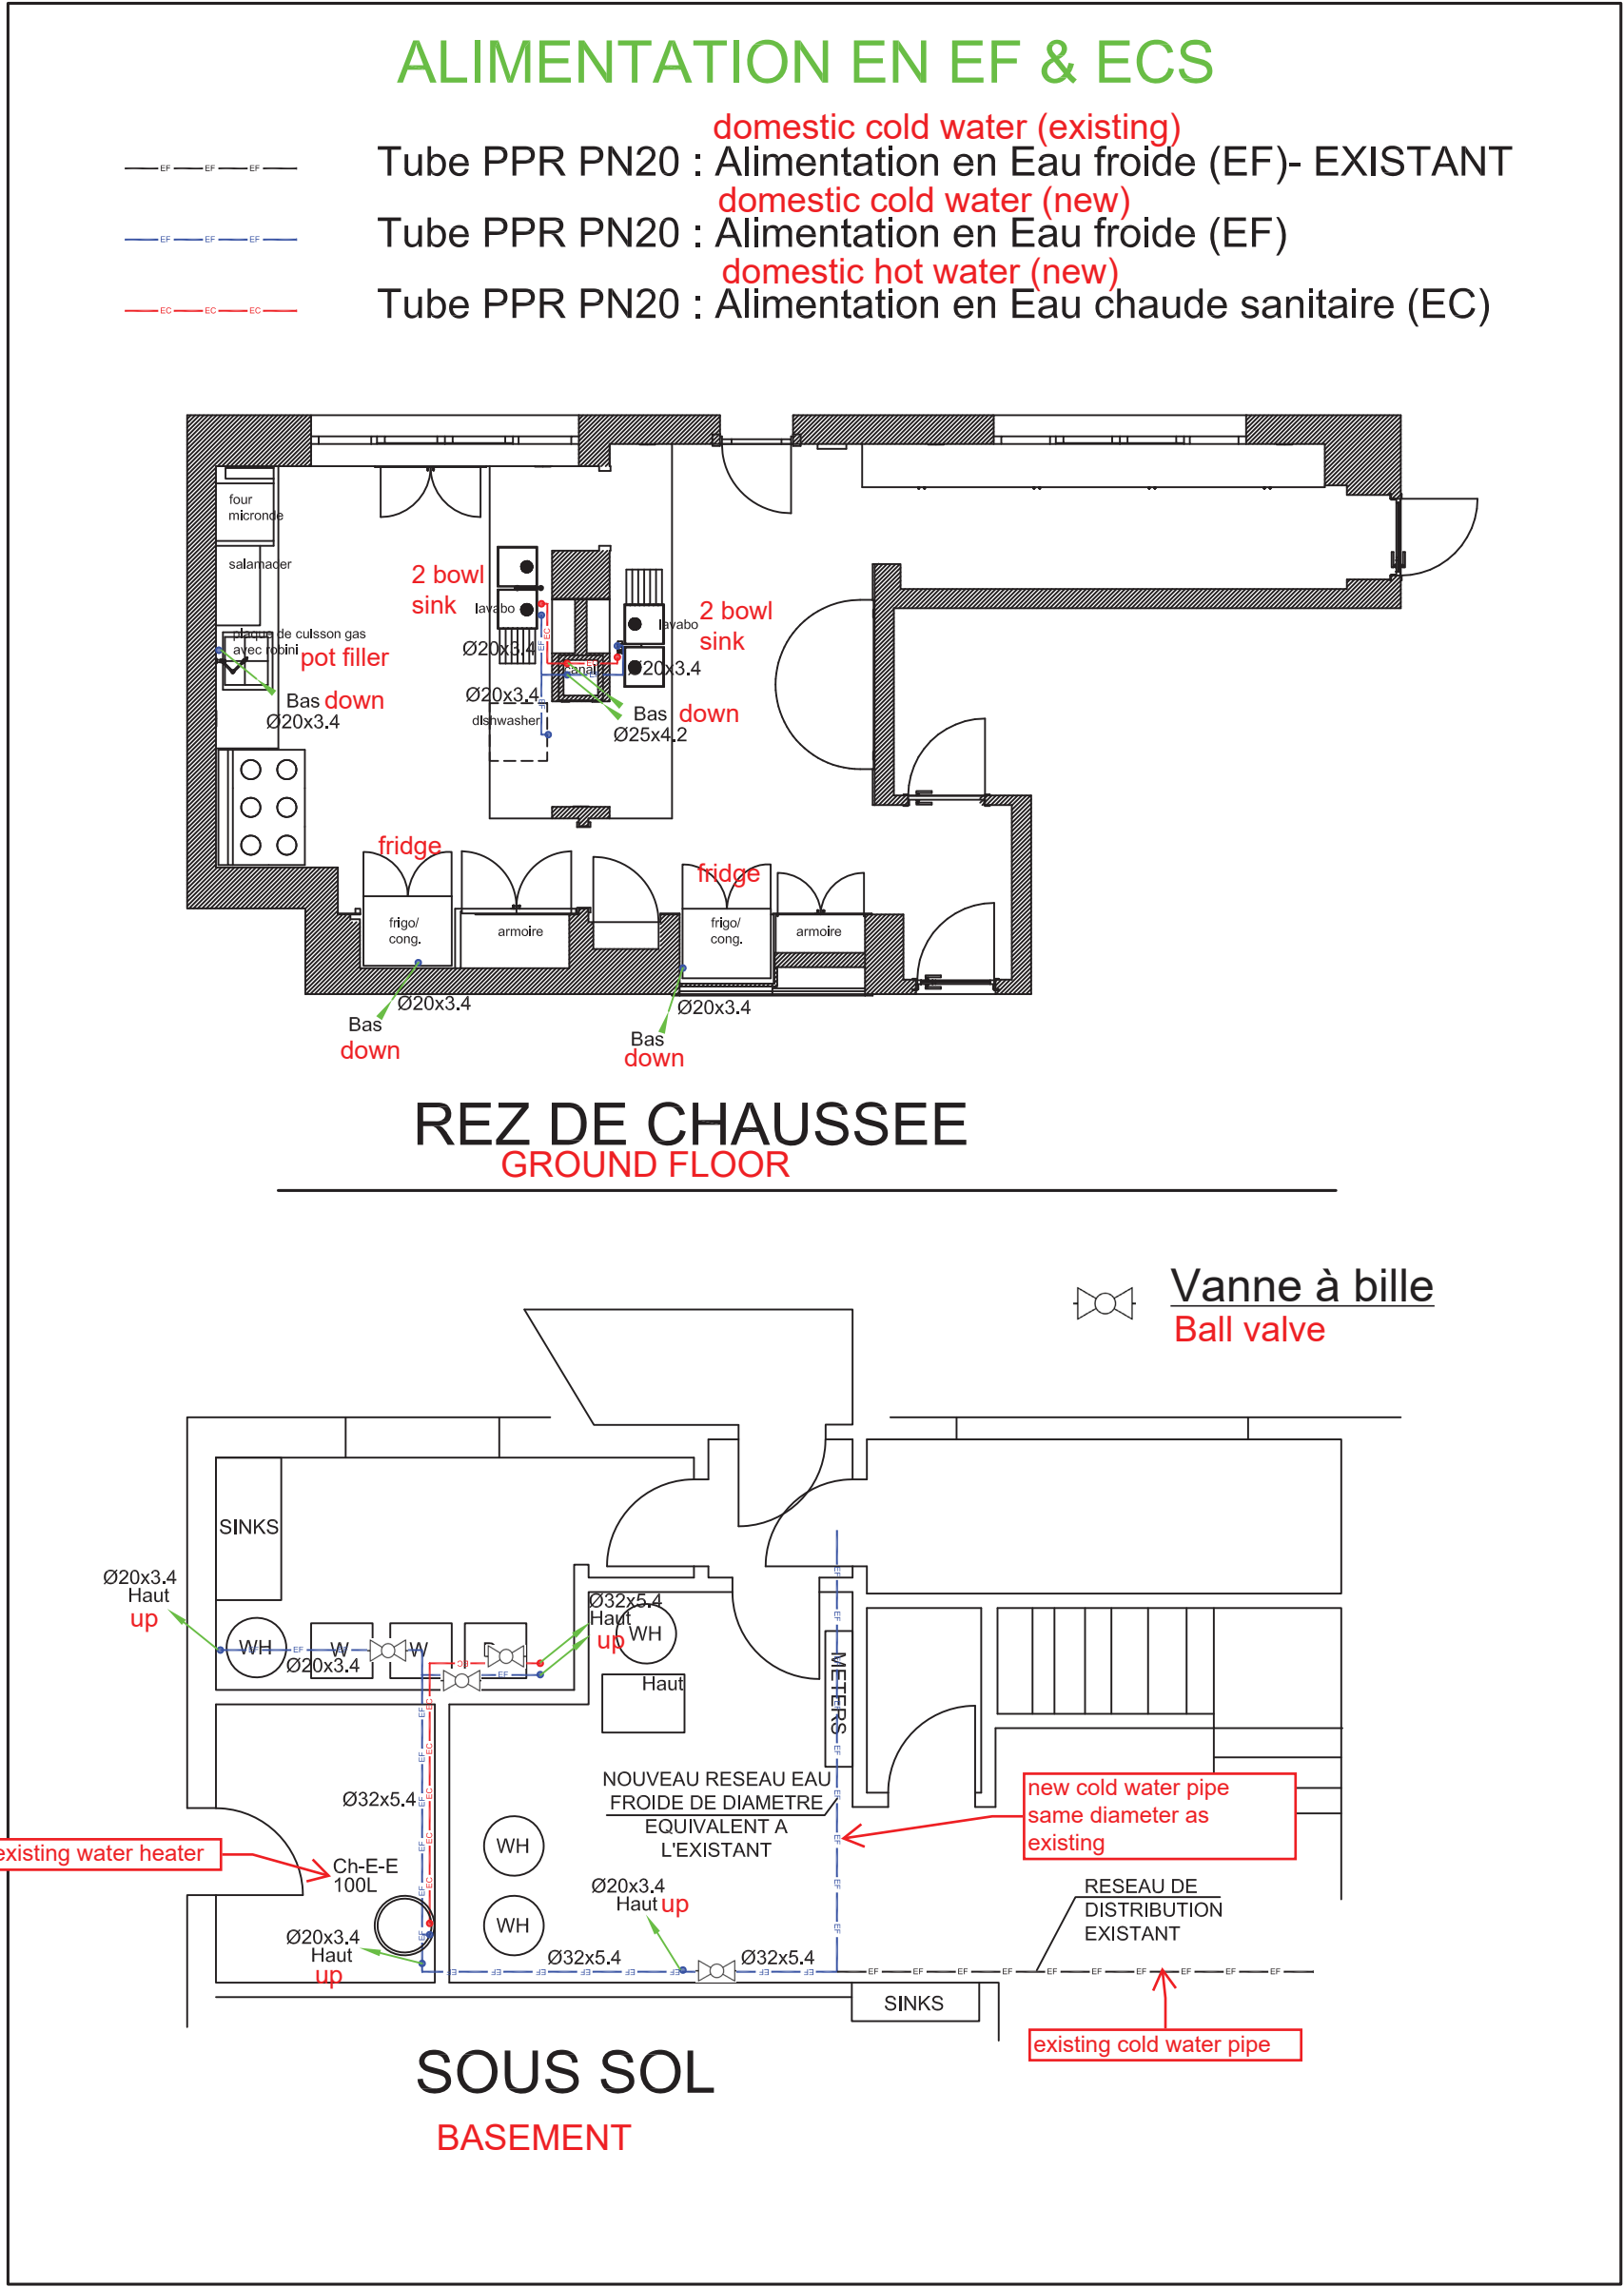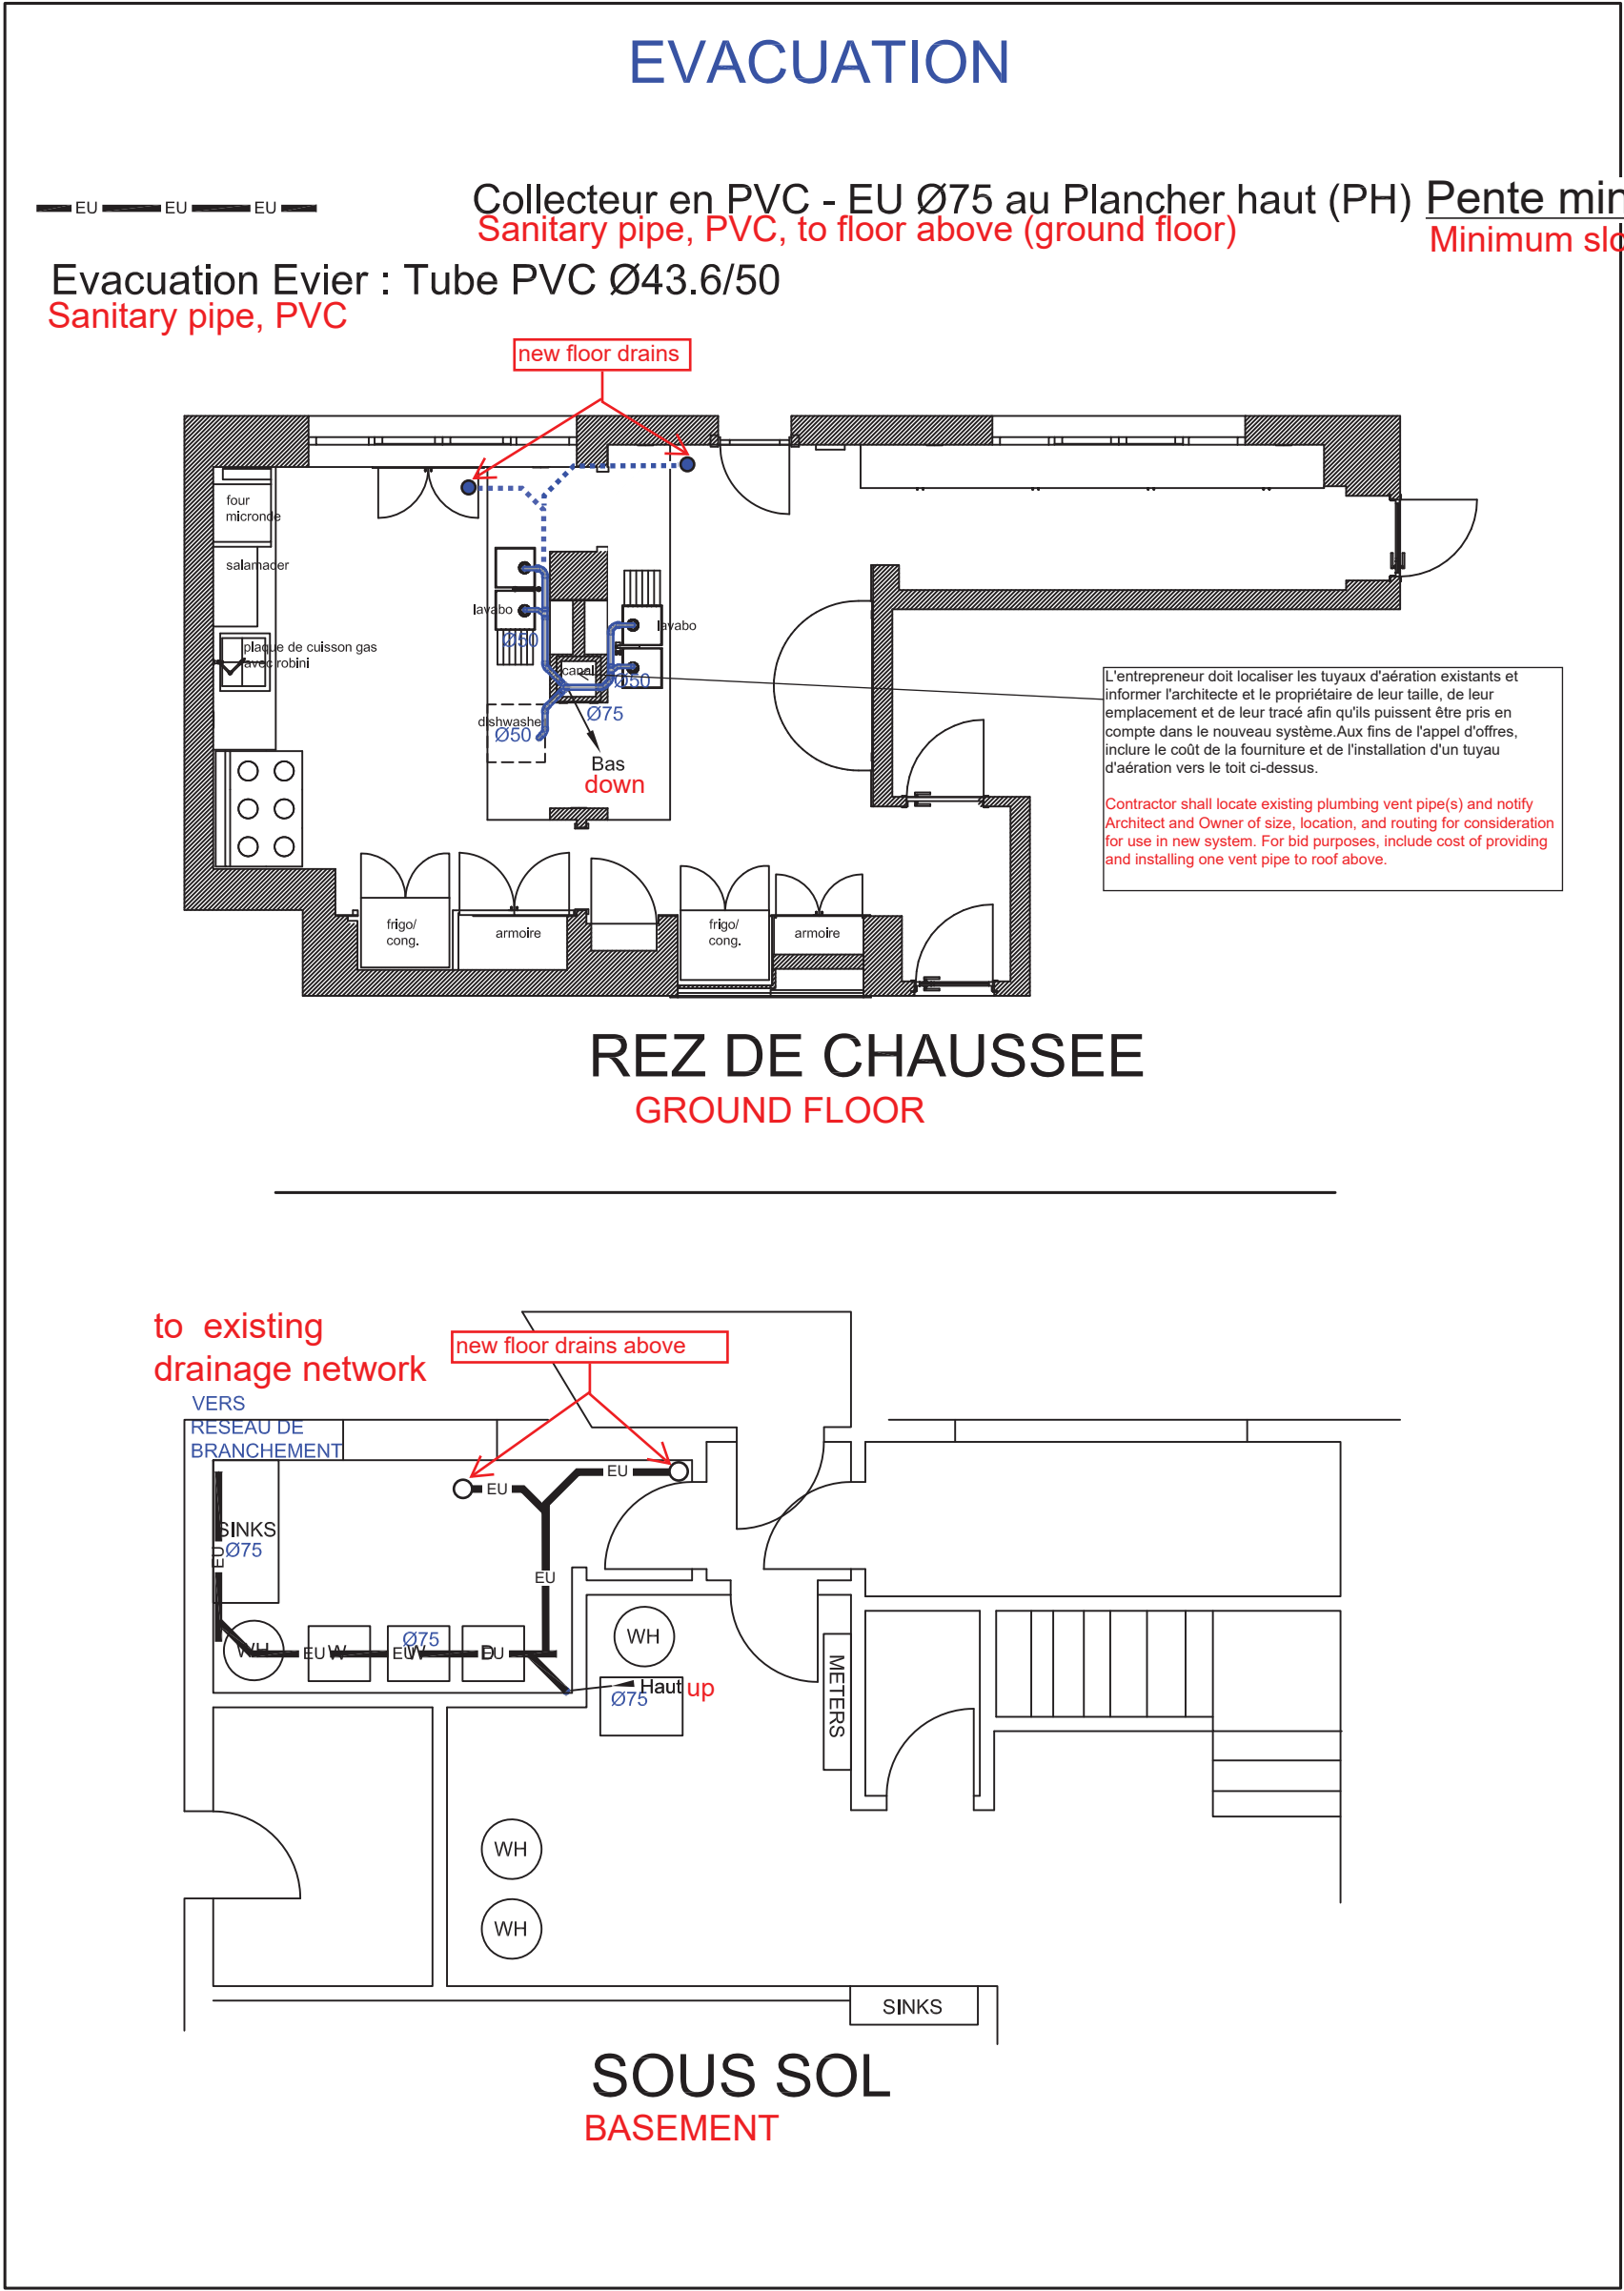

ROYAUME DU MAROC

WILAYA DE DE LA REGION

CASABLANCA - SETTAT

MAITRE D'OUVRAGE :

PROJET :

CONSUL GENERAL RESIDENCE - CASABLANCA - KITCHEN RENOVATION

ARCHITECTE :

Bureau de Contrôle :

Entreprise :

Révision	Date	Modifications – Observations	Dessiné	Vérifié	Approuvé
A	10–2024	1ère EMISSION			
B	06 JAN 2026	90% REVISION			
C	02 FEB 2026	100% FOR BID			

AO :

LOT CLIMATISATION - VMC

REZ DE CHAUSSEE,

DATE :

ECHELLE :

Client

Plan N° 01

CLIM

Indice A

AFFAIRE N°

DESSINE PAR

VERIFIE PAR

Caisson d'extraction hôte cuisine
Exterior wall mounted vent fan; see specification item No. 16

Gaine Circulaire en tole d'acier galvanisée
galvanized steel air duct; match existing size

existing wall mount mini split to remain

Split système mural existant

Hotte d'extraction existante

existing stainless steel range hood to remain

REZ DE CHAUSSEE

