



REPLY TO  
ATTENTION OF

**DEPARTMENT OF THE ARMY**  
LOUISVILLE DISTRICT, CORPS OF ENGINEERS  
P.O. BOX 59  
LOUISVILLE, KENTUCKY 40201-0059

Contracting Division

18 June 2024

Bill W. Jarrett Construction Company, Inc.  
Butts Construction Company, Inc.  
Howard W. Pence, Inc.  
PEM-Jarkins JV LLP  
Southeastern Industrial Barlovento JV-2, LLC  
Zodiac-Poettker HBZ Joint Venture, LLC  
ESA South, Inc.

Dear MATOC Contractors:

Reference is made to your Indefinite Delivery Contracts, Numbers W912QR21D0049 - W912QR21D0055, IDIQ Design Build and Design Bid Build Multiple Award Task Order Contracts (MATOC) to support the military construction (MILCON) and operations and maintenance (O&M) funded construction requirements for the U.S. Army Reserves, U.S. Air Force Reserves, U.S. Air Force, and U.S. Army programs in the Southeast Region.

Amendment 0005 for solicitation number W912QR-51061297 for the Addition/Repair of the Component Medical Training Facility, B3120, located on Eglin Air Force Base, FL, is hereby issued and incorporates the following changes.

**SUMMARY OF CHANGES:**

**1. The following SPECIFICATION SECTIONS have been revised and replaced in their entirety:**

None

**2. The following SPECIFICATION SECTIONS have been added in their entirety:**

None

**3. The following SPECIFICATION SECTIONS have been deleted in their entirety:**

None

**4. The following PLAN SHEETS have been revised and replaced in their entirety:**

|       |                                 |
|-------|---------------------------------|
| AD101 | OVERALL DEMOLITION PLAN         |
| A-101 | OVERALL FLOOR PLAN              |
| A-103 | ROOF PLAN                       |
| A-311 | WALL SECTIONS                   |
| A-401 | ENLARGED FLOOR PLAN AND DETAILS |
| A-451 | AIR BARRIER DETAILS             |
| A-452 | AIR BARRIER DETAILS             |

|        |                       |
|--------|-----------------------|
| A-571  | ROOF DETAILS          |
| CS-100 | SITE PLAN             |
| CS-110 | STAKING PLAN          |
| ED101  | ELECTRICAL DEMOLITION |

**5. The following PLAN SHEETS have been added new:**

None

**6. The following PLAN SHEETS have been deleted in their entirety new:**

None

**7. The following DOCUMENTS have been added new:**

None

**8. The proposal due date and time has changed to 2 July 2025 at 10:00 AM ET.**

Submit your proposal by email to [charity.a.mansfield@usace.army.mil](mailto:charity.a.mansfield@usace.army.mil). Proposals not received by the stated date/time will not be considered. Please acknowledge receipt of this amendment by signing below in the space provided and returning to Charity Mansfield at [charity.a.mansfield@usace.army.mil](mailto:charity.a.mansfield@usace.army.mil).

If you have contractual questions, please contact Charity Mansfield at [charity.a.mansfield@usace.army.mil](mailto:charity.a.mansfield@usace.army.mil). If an Offeror believes that the requirements in the RFP contain an error, omission, or are otherwise unsound; the offeror shall immediately notify the Contract Specialist in writing with supporting rationale. All Offerors is reminded that the Government reserves the right to award this RFP based on the initial proposals, as received, without discussion.

Sincerely,

WANTLAND.ADA  
M.M.1539936006

Digitally signed by  
WANTLAND.ADA.M.M.15399360  
06  
Date: 2025.06.18 13:36:24 -04'00'


Adam M. Wantland  
Contracting Officer

**ACKNOWLEDGEMENT OF AMENDMENT:**

\_\_\_\_\_  
(Signature) (Date)

\_\_\_\_\_  
(Printed Name)

\_\_\_\_\_  
(Firm Name)

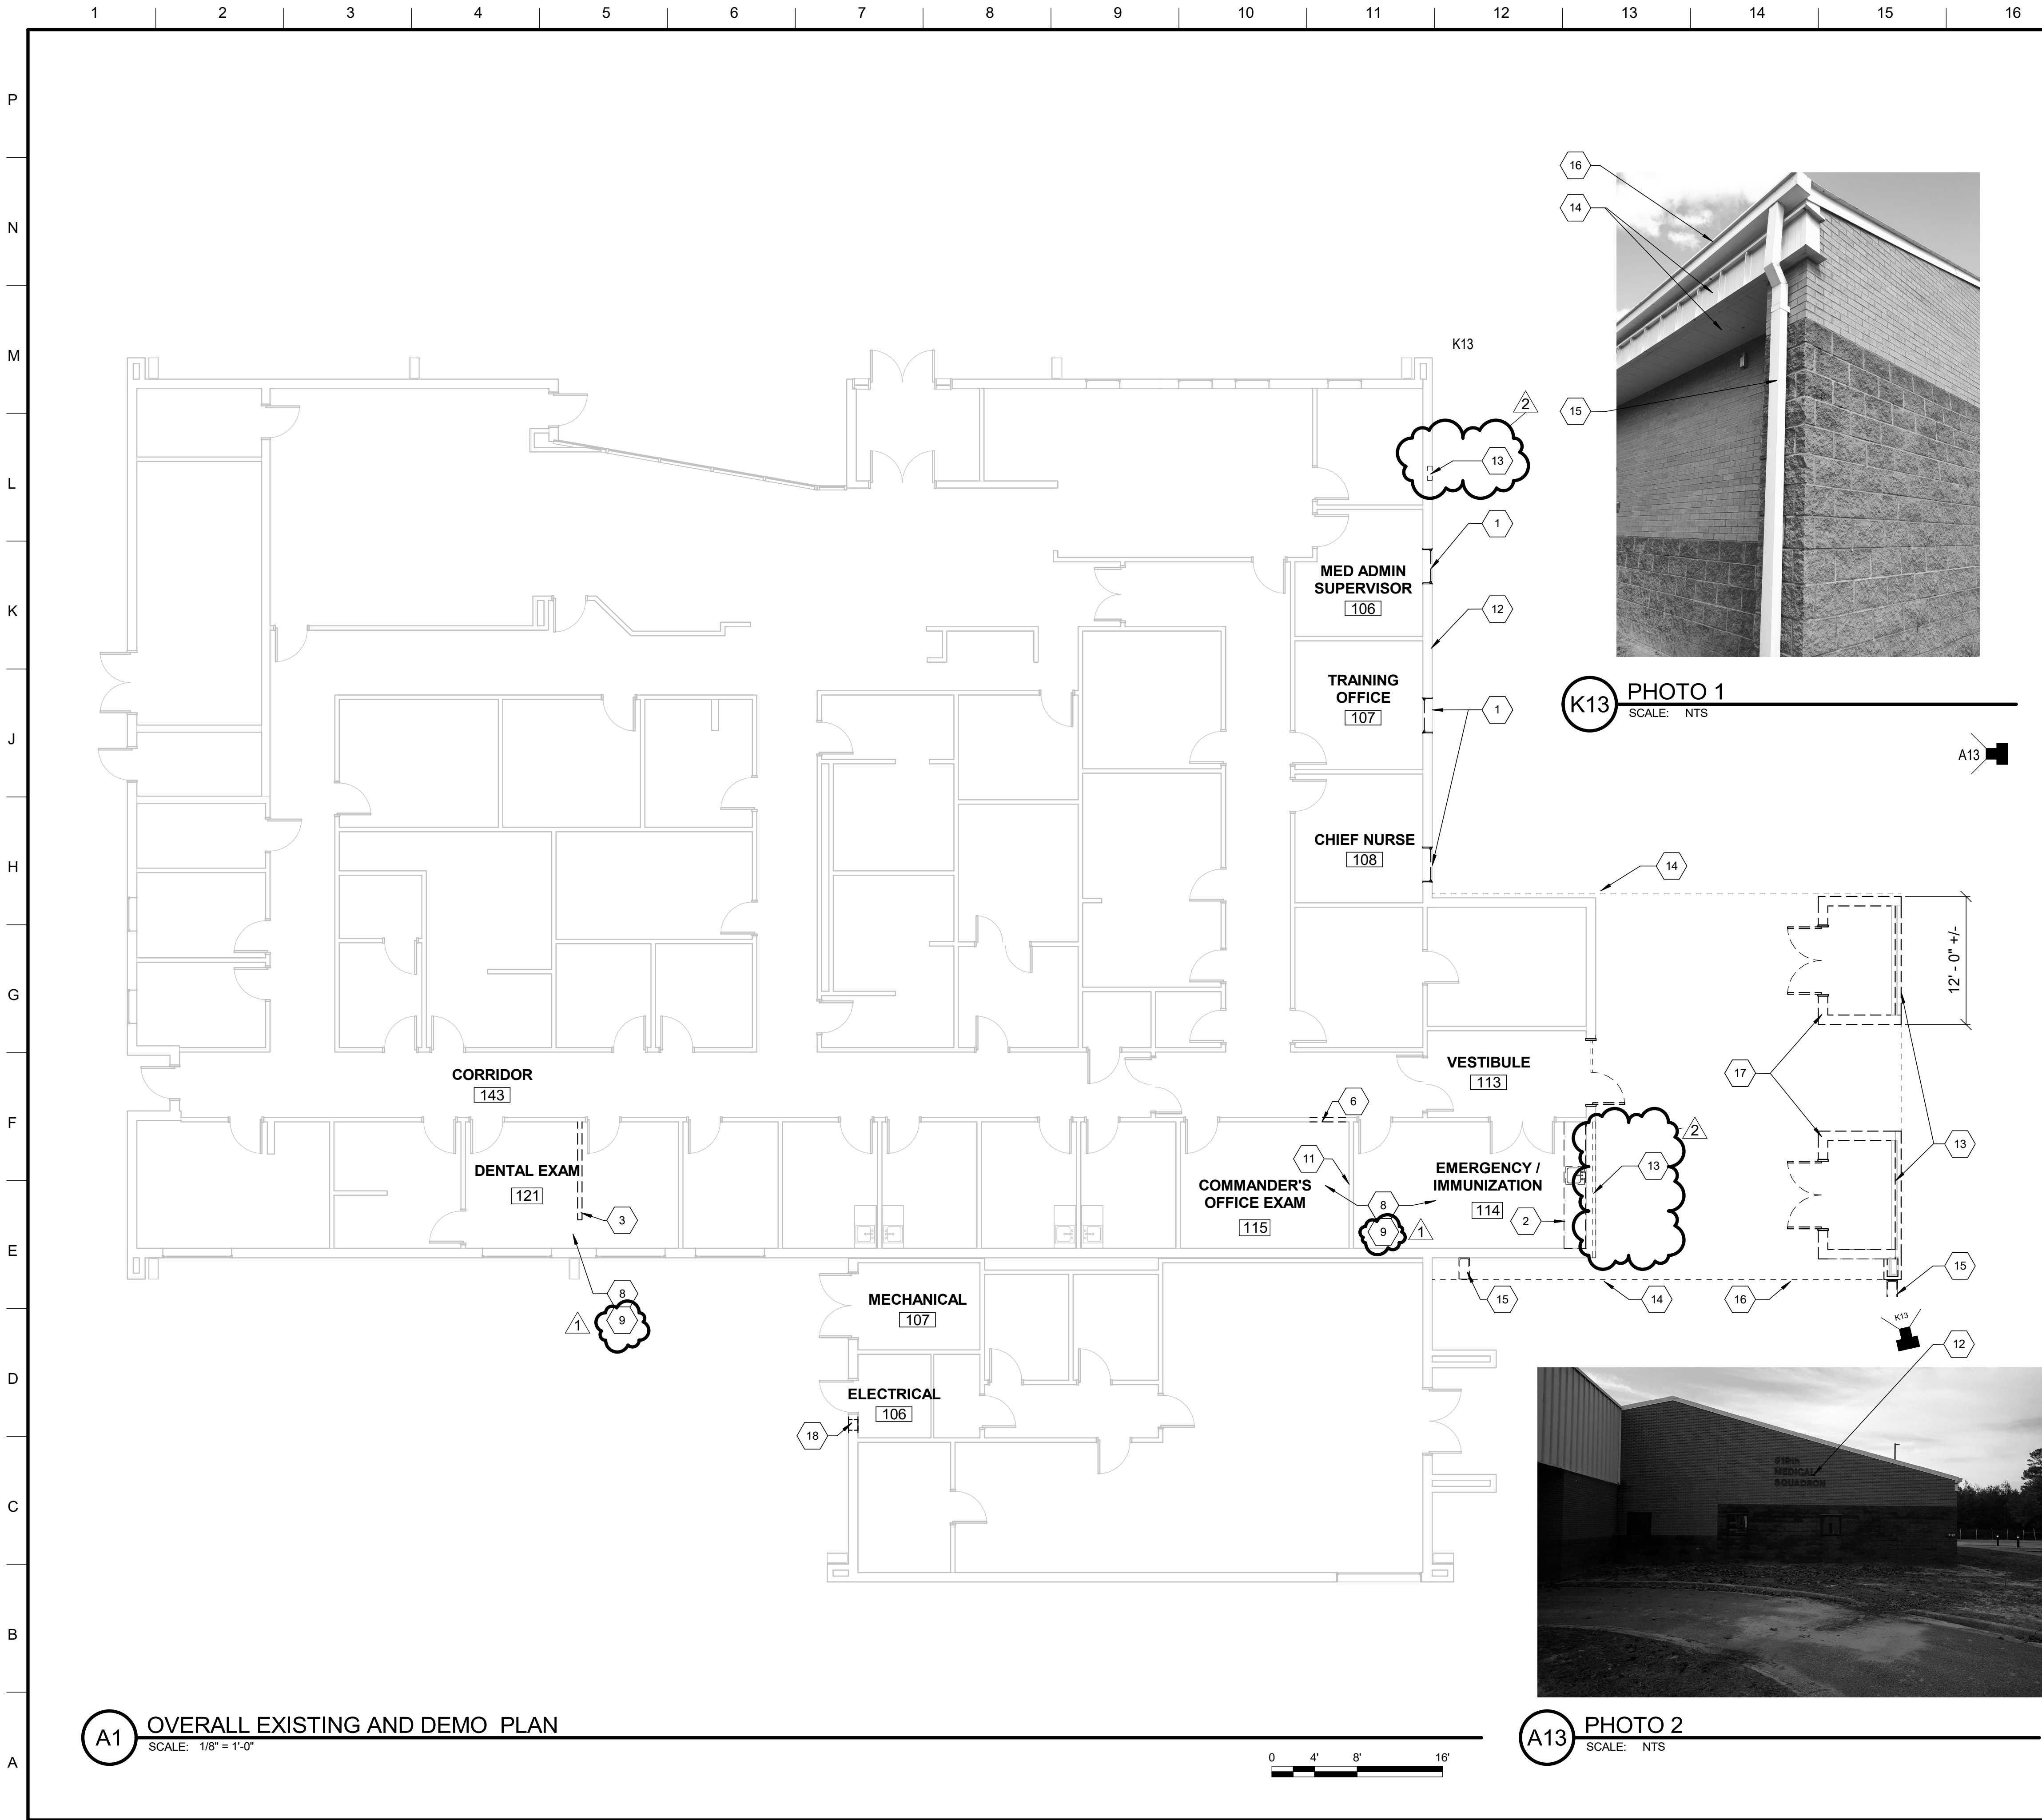


## GENERAL SHEET NOTES

- FOR ARCHITECTURAL GENERAL NOTES, MATERIAL LEGEND, AND ABBREVIATIONS REFER TO SHEET A-001.
- EXCEPT FOR ITEMS OR MATERIALS INDICATED TO BE REUSED, SALVAGED, REINSTALLED, OR OTHERWISE INDICATED TO REMAIN THE OWNER'S PROPERTY, DEMOLISHED MATERIALS BECOME THE CONTRACTOR'S PROPERTY AND MUST BE REMOVED FROM THE SITE WITH FURTHER DISPOSITION AT THE CONTRACTOR'S OPTION.
- IT IS NOT EXPECTED THAT HAZARDOUS MATERIALS WILL BE ENCOUNTERED IN THE WORK. IF MATERIALS SUSPECTED OF CONTAINING HAZARDOUS MATERIALS ARE ENCOUNTERED, DO NOT DISTURB; IMMEDIATELY NOTIFY CONTRACTING OFFICER.
- FURNITURE WILL BE REMOVED OR RELOCATED BY THE OWNER AS NECESSARY PRIOR TO THE DEMOLITION WORK OF THIS PROJECT.
- CARE SHOULD BE MADE TO KEEP DUST AND NOISE FROM DEMOLITION ACTIVITIES FROM THE OTHER PORTIONS OF THE BUILDING. ERECT AND MAINTAIN DUSTPROOF PARTITIONS. COVER AND PROTECT FURNITURE, FURNISHINGS AND EQUIPMENT THAT HAVE NOT BEEN REMOVED.
- PROVIDE TEMPORARY BARRICADES AND OTHER PROTECTION REQUIRED TO PREVENT INJURY TO PEOPLE AND DAMAGE TO ADJACENT BUILDING AREAS TO REMAIN.
- NEATLY CUT OPENINGS AND HOLES PLUMB, SQUARE AND TRUE TO DIMENSIONS REQUIRED. USE CUTTING METHODS LEAST LIKELY TO DAMAGE ADJOINING CONSTRUCTION TO REMAIN.
- AT LOCATIONS WHERE FLOORING IS TO BE DEMOLISHED, FLOOR MUST BE FREE OF DUST, DIRT, OIL, GREASE, PAINT, WAX OR ANY DEBRIS THAT COULD AFFECT INSTALLATION OF NEW FLOORING.
- DRYWALL PARTITIONS: REMOVE GYPSUM BOARD, STEEL FRAMING, RUNNERS, TRACKS, ANCHORS AND FASTENERS, UNLESS OTHERWISE NOTED OR SHOWN. PATCH ANCHOR HOLES WHERE CEILING, WALLS, AND FLOORS ARE TO REMAIN.

## SHEET KEYNOTES

- DEMOLISH WINDOWS AND INTERIOR SILLS; REPAIR FOR INTERIOR WALL. PATCH AND REPAIR TO MATCH ADJACENT MATERIAL, COLOR, AND FINISH.
- DEMOLISH EXISTING SINK AND CABINETRY
- DEMOLISH EXISTING HALF WALL PARTITION AND ASSOCIATED TRIM AND FINISHES.
- DEMOLISH PORTION OF EXISTING GYPSUM METAL STUD INTERIOR WALL. AND PREPARE OPENING FOR INSTALLATION OF NEW DOOR. PATCH AND REPAIR AROUND OPENING TO MATCH ADJACENT MATERIAL, COLOR, AND FINISH. RE: SHEET A-101 FOR OPENING DIMENSIONS.
- DEMOLISH EXISTING FLOOR FINISHES AND ASSOCIATED TRIM.
- DEMOLISH EXISTING CEILING GRID SYSTEM AND ASSOCIATED TRIM.
- DEMOLISH EXISTING WALL TO INSTALL NEW PLUMBING LINES.
- REMOVE AND SALVAGE EXISTING EXTERIOR SIGNAGE.
- DEMOLISH EXISTING VENEER, INSULATION, AND VAPOR BARRIER.
- DEMOLISH EXISTING SOFFIT AND METAL PANEL ABOVE.
- DEMOLISH PREFINISHED METAL DOWNSPOUT WITH PRECAST CONCRETE SPLASHBLOCK
- DEMOLISH EXISTING PREFINISHED GUTTER.
- DEMOLISH EXISTING EXTERIOR WALL.
- DEMOLISH PORTION OF EXISTING EXTERIOR WALL AND PREPARE OPENING FOR INSTALLATION OF NEW LOUVER. PATCH AND REPAIR AROUND OPENING TO MATCH ADJACENT MATERIAL, COLOR, AND FINISH. RE: SHEET A-601 FOR OPENING DIMENSIONS.

FOR BIDDING  
ONLY  
NOT FOR  
CONSTRUCTION

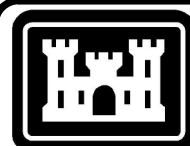

US Army Corps  
of Engineers ®

| DATE       | DESCRIPTION                               | MARK |
|------------|-------------------------------------------|------|
| 09/16/2025 | REVISED IN ACCORDANCE WITH AMENDMENT 0005 | 2    |
| 09/02/2025 | REVISED IN ACCORDANCE WITH AMENDMENT 0004 | 1    |

|                                |                            |                   |               |
|--------------------------------|----------------------------|-------------------|---------------|
| DESIGNED BY:<br>C. WEISBERG    | ISSUE DATE:<br>AUGUST 2024 | SOLICITATION NO.: | CONTRACT NO.: |
| DRAWN BY:<br>B. RICHARDSON     |                            |                   |               |
| CHECKED BY:<br>L. SUNDERLAND   |                            |                   |               |
| SUBMITTED BY:<br>V. BREDDICKAS |                            |                   |               |
| SIZE:<br>P2 #                  | ANSI D<br>1513409          |                   |               |


US ARMY CORPS OF ENGINEERS  
LOUISVILLE  
600 DR MARTIN LUTHER KING PL, STE 872  
LOUISVILLE, KY 40202

**BURNS  
MEDONNELL**

|   |                         |
|---|-------------------------|
| ADD REPAIR RESERVE COMPONENT MEDICAL<br>TRAINING FACILITY B3120<br>PROJ NO. FTFA20CB09<br>P2#: 513409 | OVERALL DEMOLITION PLAN |
|---|-------------------------|

|          |
|----------|
| SHEET ID |
| AD101    |



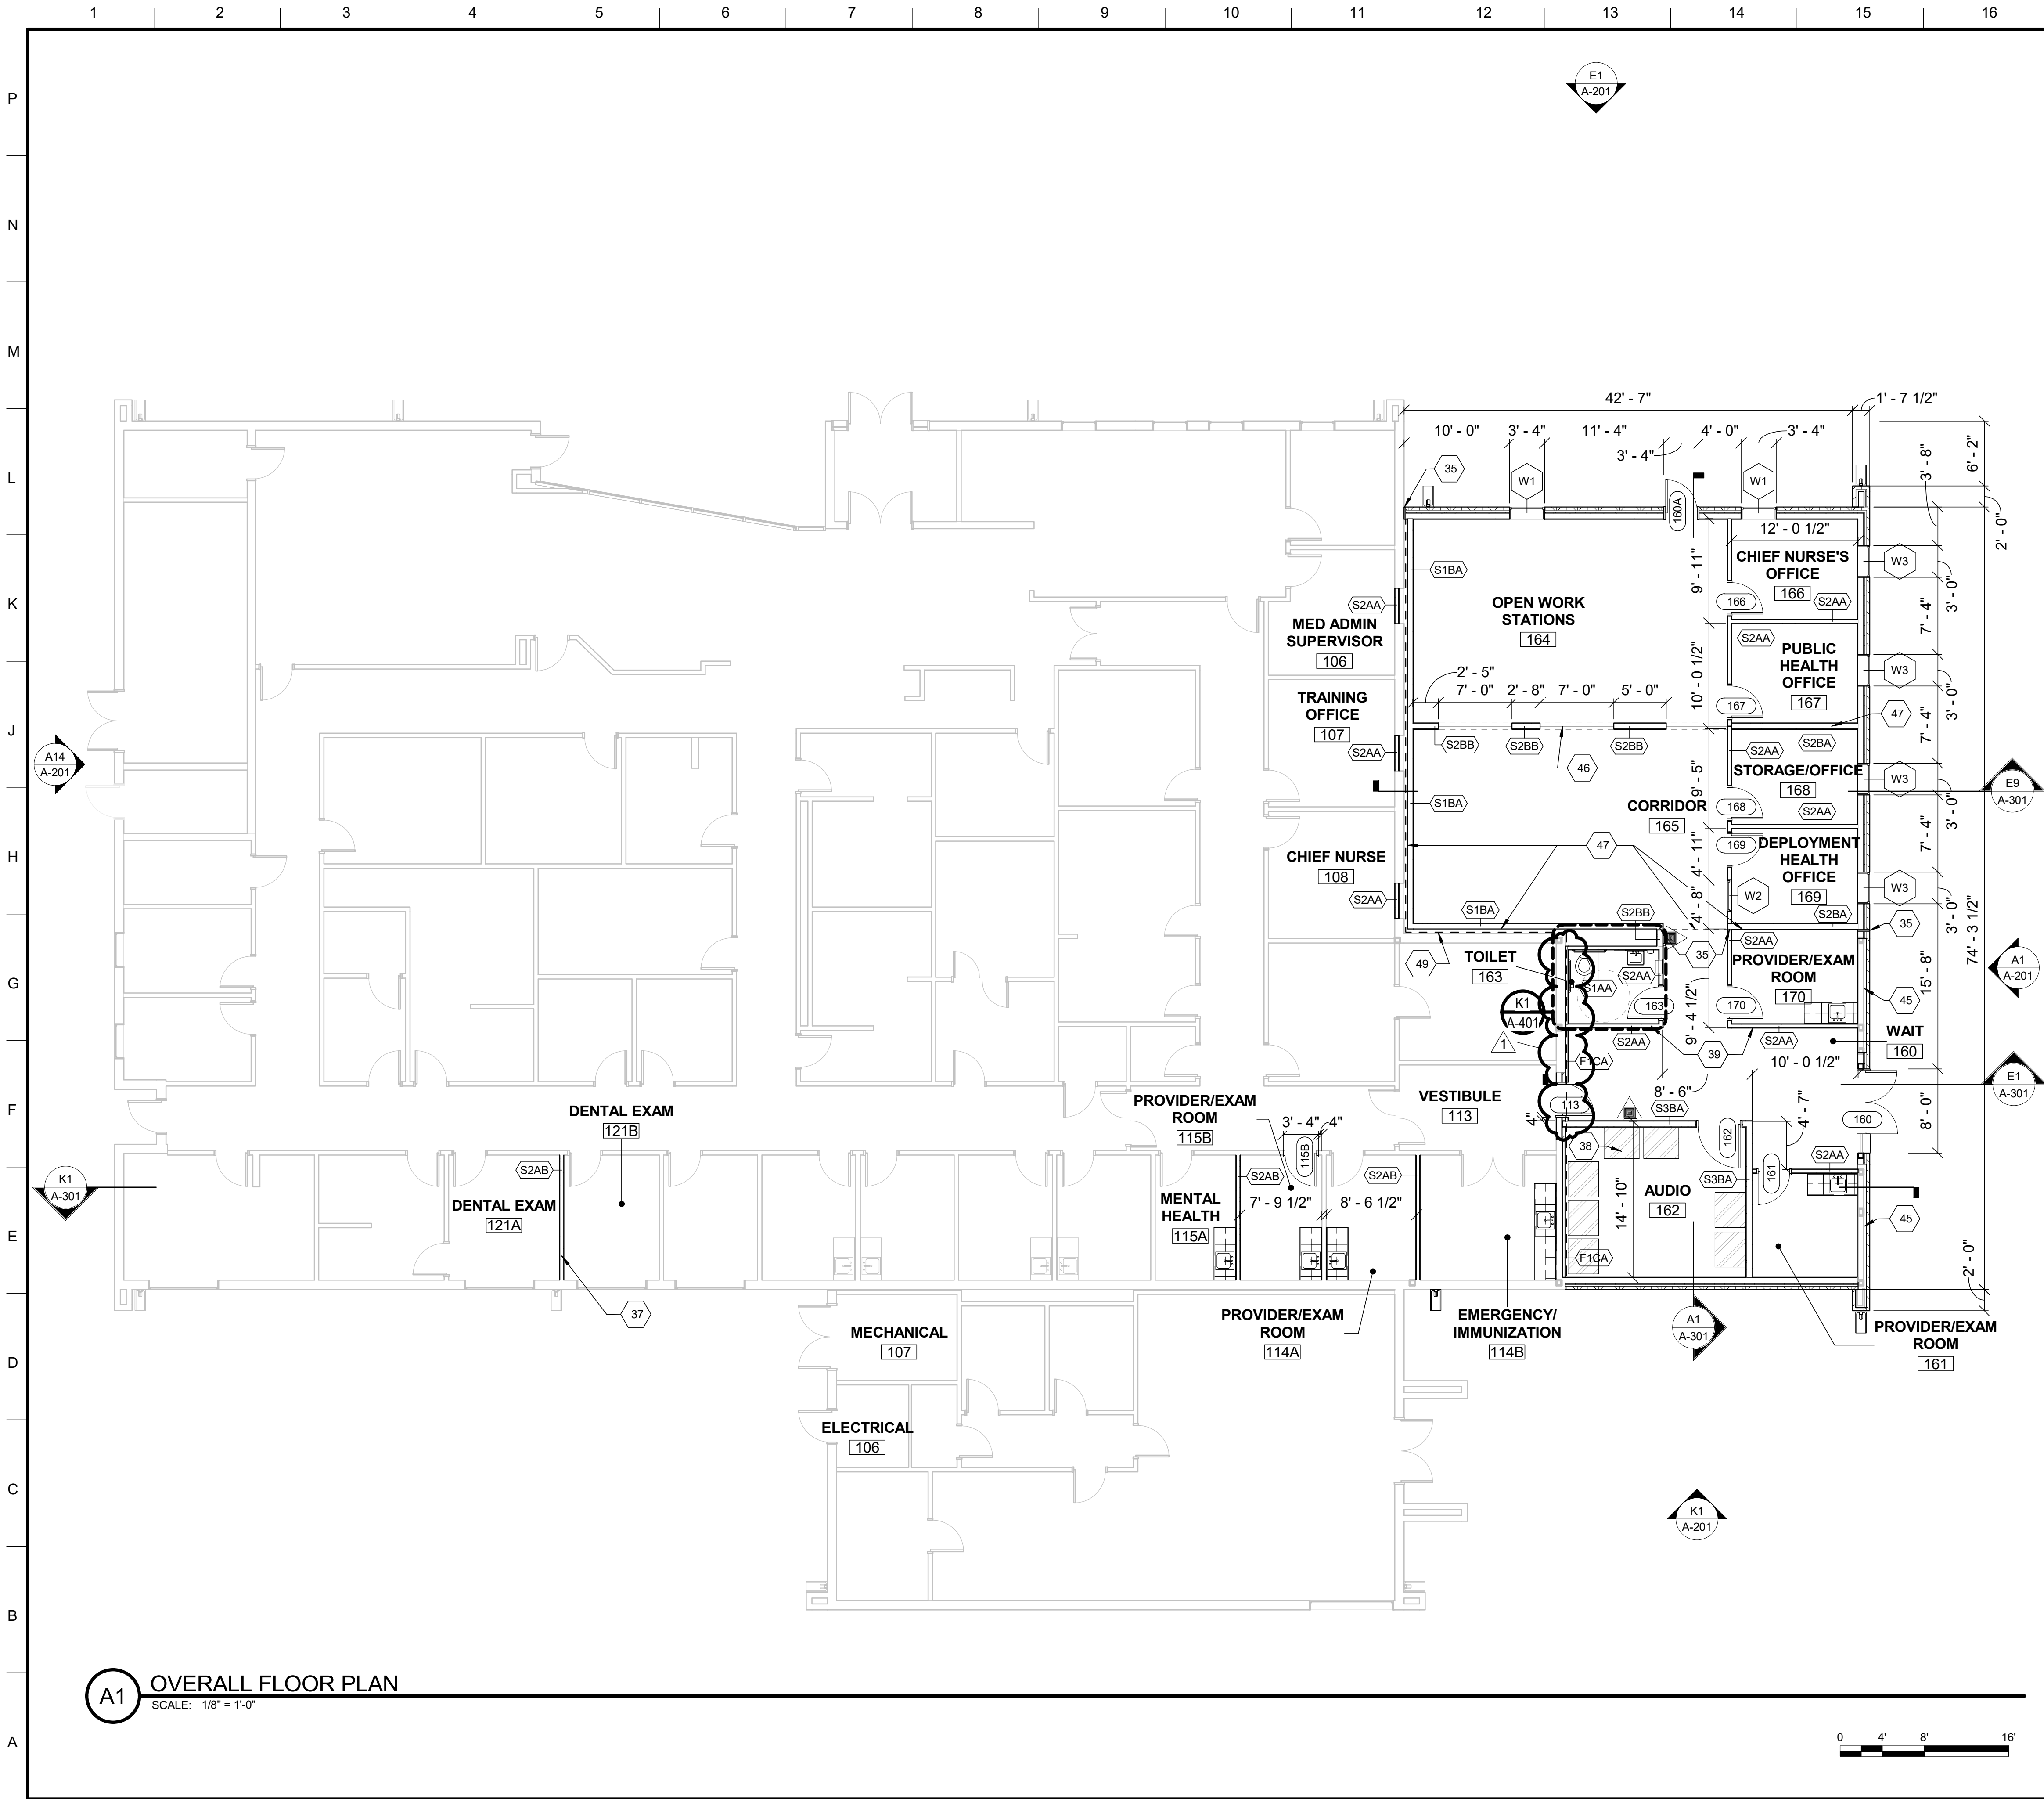

## GENERAL SHEET NOTES

- FOR ARCHITECTURAL GENERAL NOTES, MATERIAL LEGEND, AND ABBREVIATIONS REFER TO SHEET A-001.
- FOR PARTITION TYPES CONSTRUCTION AND DESCRIPTION REFER TO PARTITION TYPES SHEET.
- FOR DIMENSIONS OR ADDITIONAL INFORMATION NOT ILLUSTRATED, REFER TO LARGER SCALE DRAWINGS.
- DOOR LOCATIONS NOT DIMENSIONED ARE 4 INCHES FROM FACE OF GYPSUM BOARD FINISH WALL TO DOOR JAMB FACE. VERIFY THERE IS A PULL SIDE MINIMUM 18 INCHES CLEAR FROM DOOR STRIKE TO INTERSECTING WALL FOR ABA COMPLIANCE. NOTIFY CONTRACTING OFFICER FOR NON-COMPLIANCE BEFORE SETTING DOOR FRAME AND WALL LOCATIONS.
- PROVIDE MILLWORK TRIM AND INFILL PANELS AT UNDERCOUNTER / CABINET LOCATIONS.
- REFER TO FINISH SCHEDULE AND FINISH PLANS FOR ADDITIONAL FINISH INFORMATION. FLOOR FINISHES TO BE CONTINUOUS UNDER MILLWORK AND EQUIPMENT UNLESS NOTED OTHERWISE.
- PROVIDE 18GA METAL PLATE OR FIRE TREATED WOOD BLOCKING IN WALL FOR TOILET FIXTURES, ACCESSORIES, EQUIPMENT, FLOOR AND WALL MOUNTED TOILET PARTITIONS, WALL STOPS, AND COUNTERTOP MOUNTING SUPPORTS.
- REFER TO SPECIFICATIONS FOR LOCATIONS OF GYPSUM BOARD CONTROL JOINTS.
- FOR EXPANSION JOINT DETAILS, REFER TO SHEET A-451 AND A-571.
- REFERENCE THE REFLECTED CEILING PLANS FOR CEILING HEIGHTS.
- DIMENSIONS ARE FROM: COLUMN GRID LINE, FACE OF EXISTING WALL, AND FACE OF METAL STUD, UNLESS NOTED OTHERWISE.
- THE FIRST FLOOR FINISHED FLOOR ELEVATION IS 100'-0" UNLESS NOTED OTHERWISE.
- REFERENCE FURNITURE PLANS FOR LOCATIONS OF WALL ACCESSORIES AND VISUAL DISPLAY EQUIPMENT. PROVIDE BLOCKING AS REQUIRED.
- REFER TO SHEET A-010 FOR EXTERIOR WALL DETAIL CALLOUTS.


## SHEET KEYNOTES

- |    |                                                            |
|----|------------------------------------------------------------|
| 35 | 2" BUILDING EXPANSION JOINT                                |
| 37 | MATCH EXISTING WALL LOCATION                               |
| 38 | AUDIO TESTING BOOTH GFGI                                   |
| 39 | ALIGN WALLS.                                               |
| 45 | SALVAGED METAL STUD PORTION OF EXISTING WALL.              |
| 46 | LOAD BEARING WALL WITH PUNCHED OPENINGS UP TO 8'-0" A.F.F. |
| 47 | LOAD BEARING WALL.                                         |
| 49 | FLUID-APPLIED AIR BARRIER AGAINST EXISTING SHEATHING.      |

## LEGEND

- |                       |                                      |
|-----------------------|--------------------------------------|
|                       | EXTINGUISHER                         |
| FE: FIRE EXTINGUISHER |                                      |
|                       | A: B: C: TYPE DRY CHEMICAL 4A-20B: C |

\*\*ALL FIRE EXTINGUISHER CABINETS MUST BE FULLY RECESSED AND MUST NOT ENCR OACH ON CORRIDOR CLEARANCE REQUIREMENTS

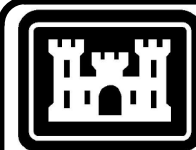

US Army Corps  
of Engineers ®

| DATE       | DESCRIPTION                               | MARK |
|------------|-------------------------------------------|------|
| 09/16/2025 | REVISED IN ACCORDANCE WITH AMENDMENT 0005 | 1    |

|                               |                            |                   |                  |
|-------------------------------|----------------------------|-------------------|------------------|
| DESIGNED BY:<br>C. WIESBERG   | ISSUE DATE:<br>AUGUST 2024 | SOLICITATION NO.: | CONTRACT NO.:    |
| DRAWN BY:<br>B. RICHARDSON    |                            |                   |                  |
| CHECKED BY:<br>L. SUNDERLAND  |                            | PROJECT NO.:      | FTFA20CB09       |
| SUBMITTED BY:<br>V. BREDICKAS |                            | SIZE:             | P2 #:<br>1513409 |
| ANSI D                        |                            |                   |                  |

US ARMY CORPS OF ENGINEERS  
LOUISVILLE  
600 DR MARTIN LUTHER KING PL, STE 872  
LOUISVILLE, KY 40202

**BURNS  
MEDONNELL**

|   |
|---|
| ADD REPAIR RESERVE COMPONENT MEDICAL<br>TRAINING FACILITY B3120<br>PROJ NO. FTFA20CB09<br>P2# 513409 |
| OVERALL FLOOR PLAN                                                                                   |

|          |
|----------|
| SHEET ID |
| A-101    |


FOR BIDDING  
ONLY  
NOT FOR  
CONSTRUCTION









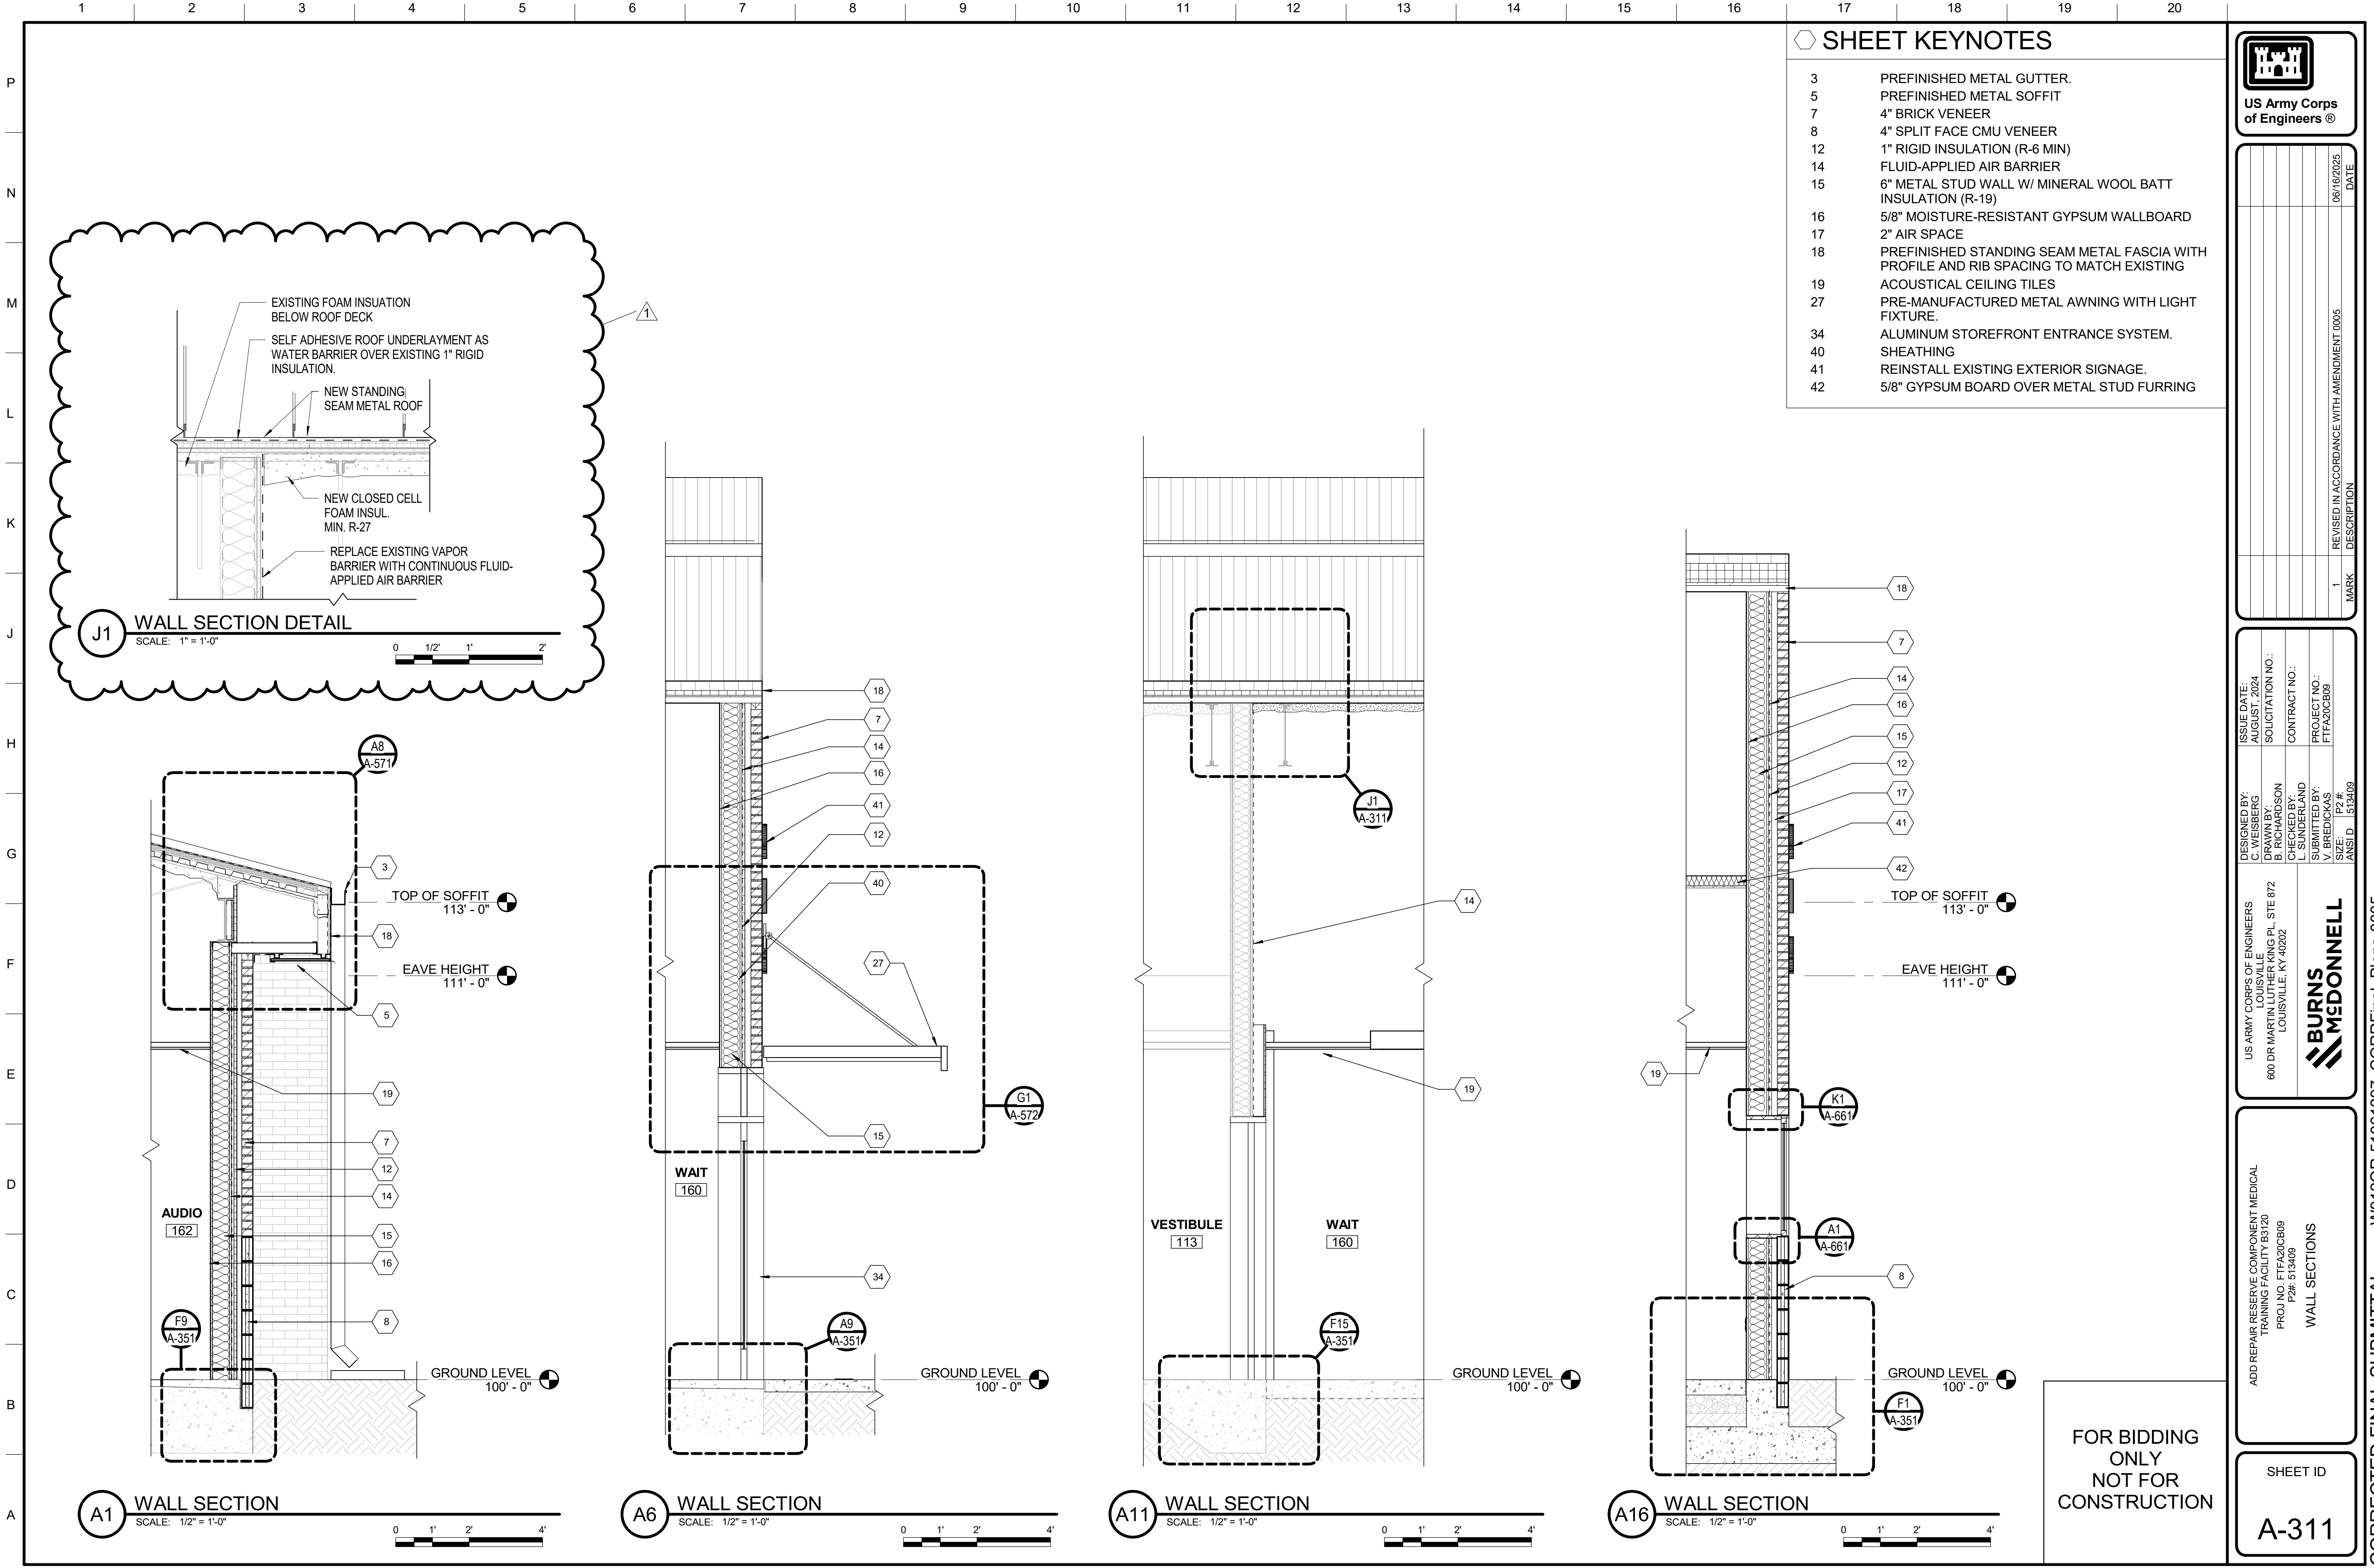

| SHEET KEYNOTES |                                                                                       |
|----------------|---------------------------------------------------------------------------------------|
| 3              | PREFINISHED METAL GUTTER.                                                             |
| 5              | PREFINISHED METAL SOFFIT                                                              |
| 7              | 4" BRICK VENEER                                                                       |
| 8              | 4" SPLIT FACE CMU VENEER                                                              |
| 12             | 1" RIGID INSULATION (R-6 MIN)                                                         |
| 14             | FLUID-APPLIED AIR BARRIER                                                             |
| 15             | 6" METAL STUD WALL W/ MINERAL WOOL BATT INSULATION (R-19)                             |
| 16             | 5/8" MOISTURE-RESISTANT GYPSUM WALLBOARD                                              |
| 17             | 2" AIR SPACE                                                                          |
| 18             | PREFINISHED STANDING SEAM METAL FASCIA WITH PROFILE AND RIB SPACING TO MATCH EXISTING |
| 19             | ACOUSTICAL CEILING TILES                                                              |
| 27             | PRE-MANUFACTURED METAL AWNING WITH LIGHT FIXTURE.                                     |
| 34             | ALUMINUM STOREFRONT ENTRANCE SYSTEM.                                                  |
| 40             | SHEATHING                                                                             |
| 41             | REINSTALL EXISTING EXTERIOR SIGNAGE.                                                  |
| 42             | 5/8" GYPSUM BOARD OVER METAL STUD FURRING                                             |

US Army Corps  
of Engineers®

|                               |                            |                                           |
|-------------------------------|----------------------------|-------------------------------------------|
| DESIGNED BY:<br>C. WEISBERG   | ISSUE DATE:<br>AUGUST 2024 | PROJECT NO.:<br>FTFA20CB09                |
| DRAWN BY:<br>B. RICHARDSON    | SOLICITATION NO.:          | MARK                                      |
| CHECKED BY:<br>L. SUNDERLAND  | CONTRACT NO.:              | 1                                         |
| SUBMITTED BY:<br>V. BREDICKAS | PROJECT NO.:               | REVISED IN ACCORDANCE WITH AMENDMENT 0005 |
| SIZE:<br>P2 #                 | ANSI D                     | DATE<br>08/16/2025                        |

US ARMY CORPS OF ENGINEERS  
LOUISVILLE  
600 DR MARTIN LUTHER KING PL, STE 872  
LOUISVILLE, KY 40202

**BURNS  
& MCDONNELL**

ADD REPAIR RESERVE COMPONENT MEDICAL  
TRAINING FACILITY B3120  
PROJ NO. FTFA20CB09  
P2# 513409

WALL SECTIONS

SHEET ID

**A-311**

CORRECTED FINAL SUBMITTAL



W912QR-51061297 CORRFinal\_Plan-0005

FOR BIDDING  
ONLY  
NOT FOR  
CONSTRUCTION







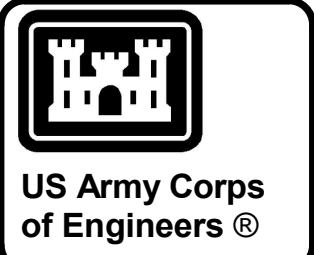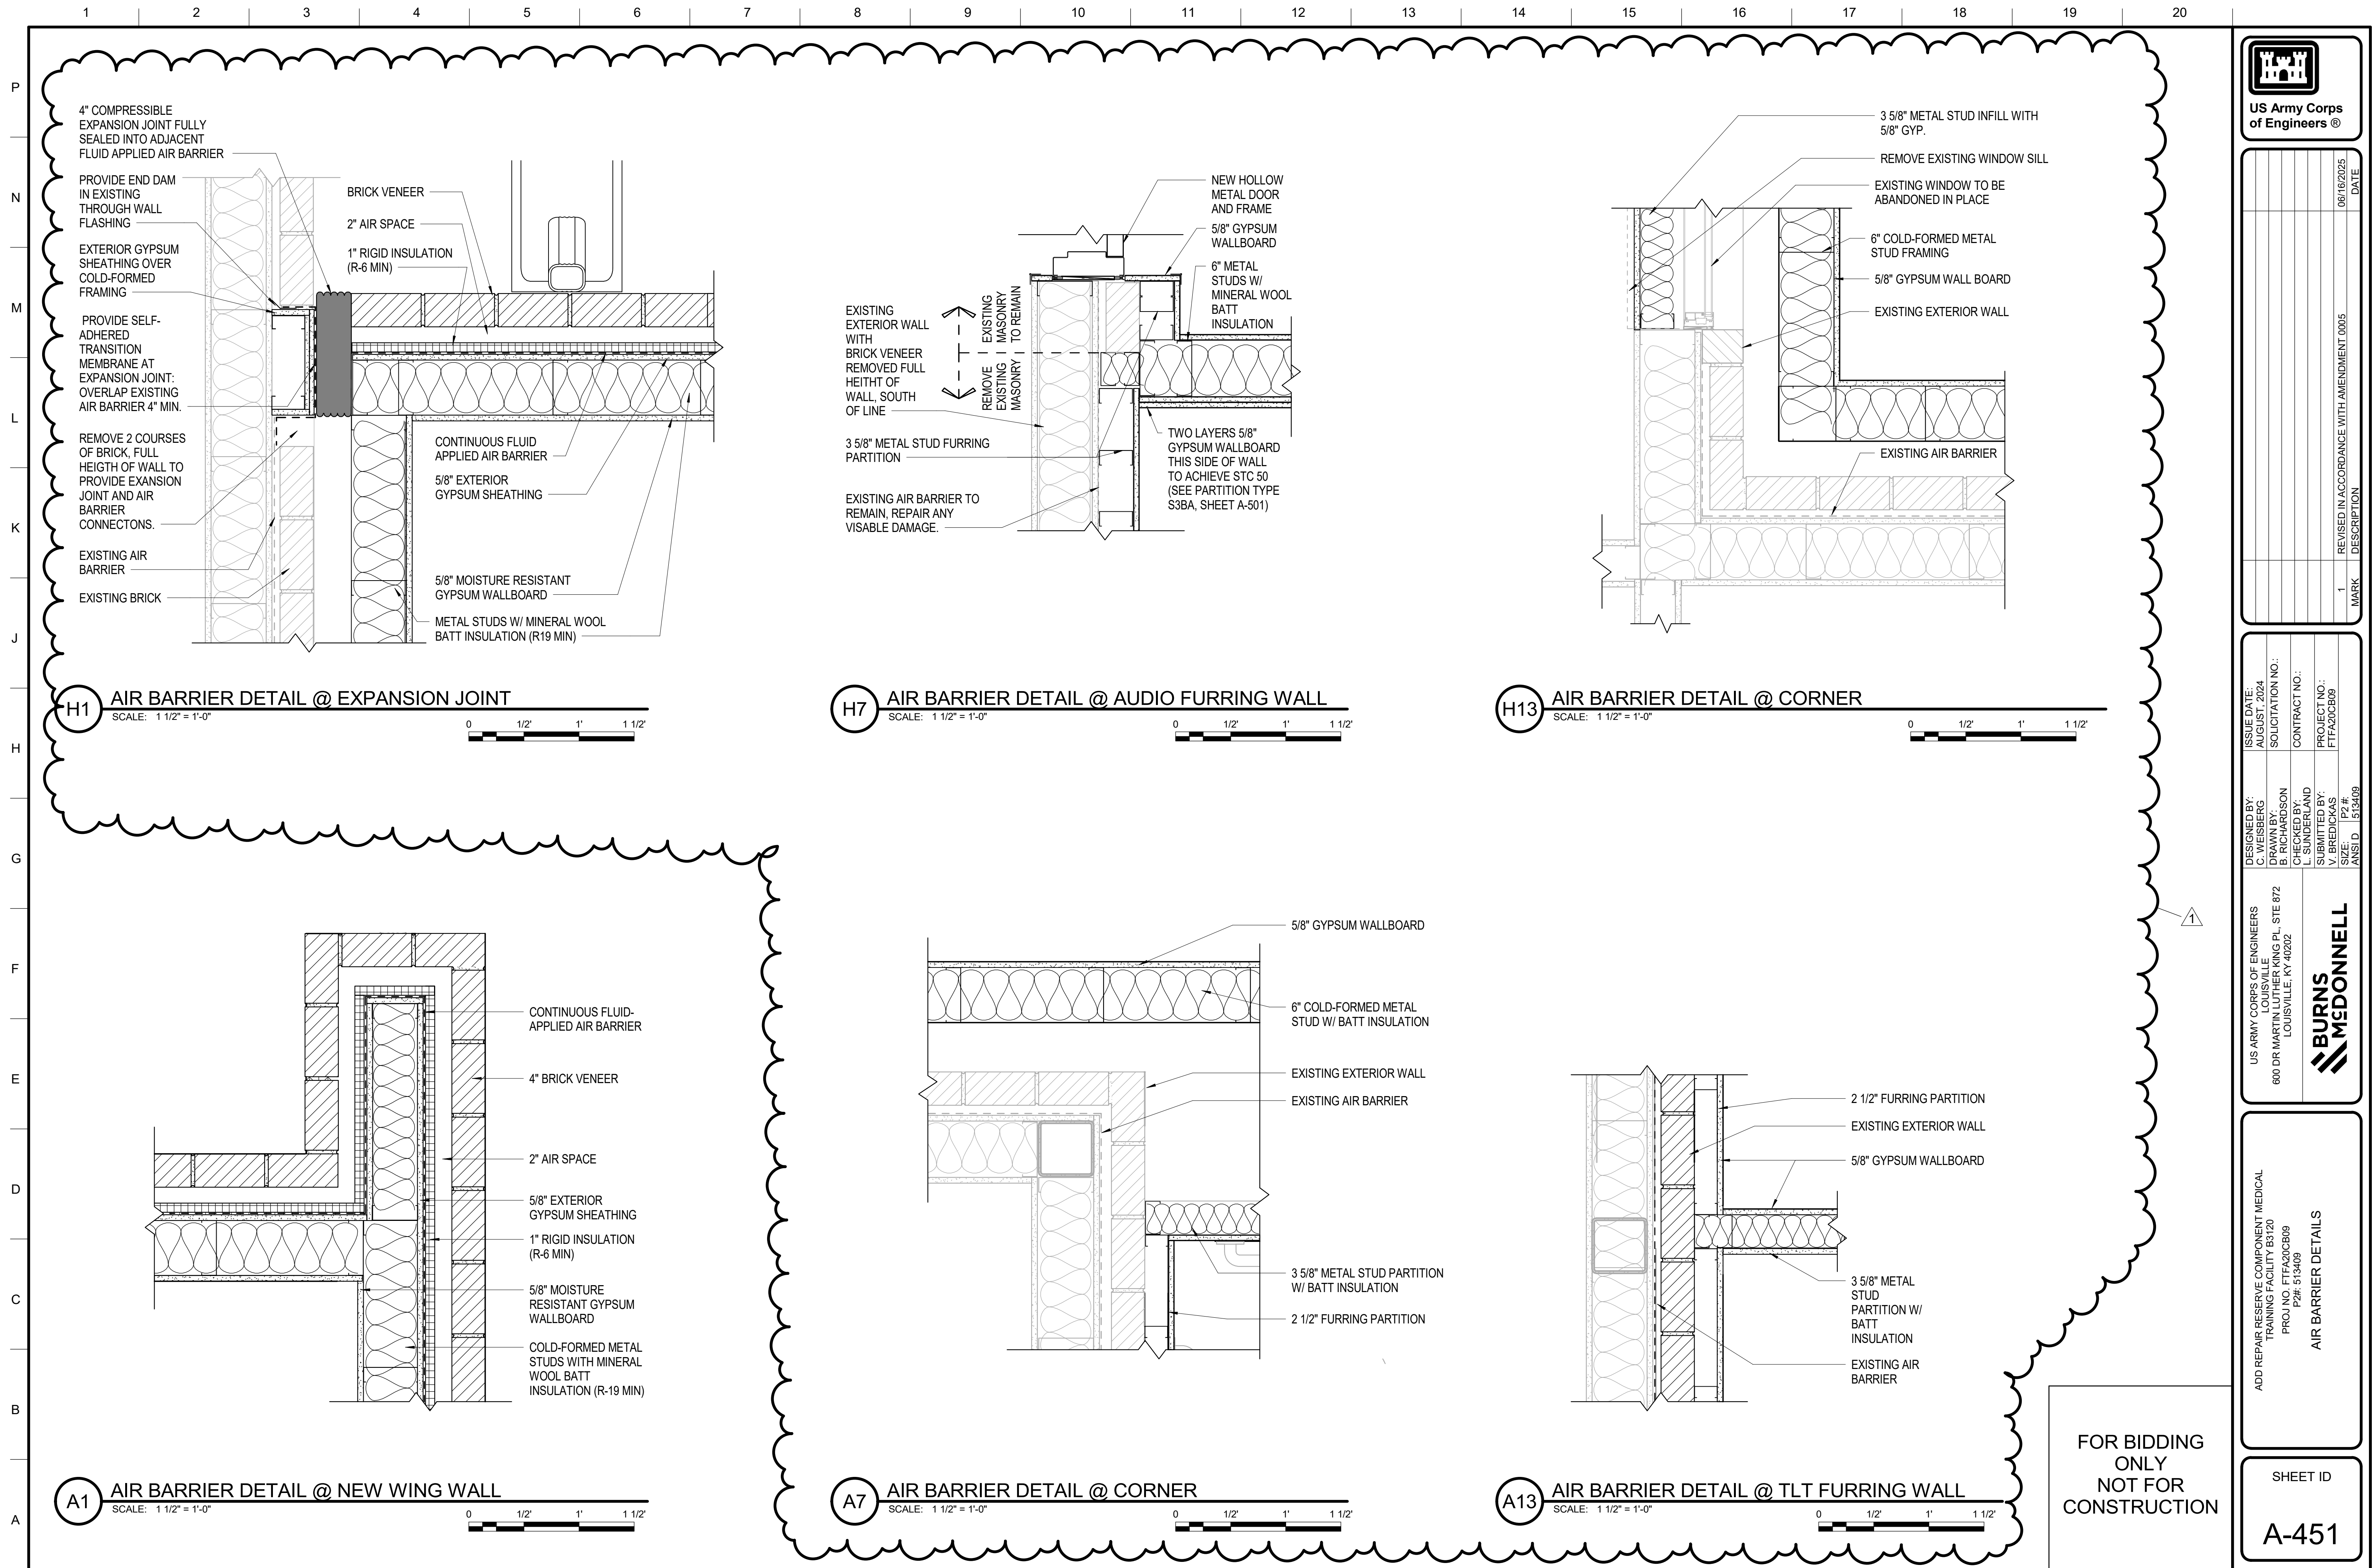

|                                            |      |            |
|--------------------------------------------|------|------------|
| REVISION IN ACCORDANCE WITH AMENDMENT 0005 |      | 08/16/2025 |
| 1                                          | MARK | DATE       |

|                               |                            |
|-------------------------------|----------------------------|
| DESIGNED BY:<br>C. WEISBERG   | ISSUE DATE:<br>AUGUST 2024 |
| DRAWN BY:<br>B. RICHARDSON    | SOLICITATION NO.:          |
| CHECKED BY:<br>L. SUNDERLAND  | CONTRACT NO.:              |
| SUBMITTED BY:<br>V. BREDICKAS | PROJECT NO.:               |
| SIZE:<br>ANSI D               | P2 #:<br>1513409           |


US ARMY CORPS OF ENGINEERS  
LOUISVILLE  
600 DR MARTIN LUTHER KING PL, STE 872  
LOUISVILLE, KY 40202

**BURNS**  
**MEDONNELL**

|   |
|---|
| ADD REPAIR RESERVE COMPONENT MEDICAL<br>TRAINING FACILITY B3120<br>PROJ NO. FTFA20CB09<br>P2#: 513409 |
|---|

|                          |
|--------------------------|
| SHEET ID<br><b>A-451</b> |
|--------------------------|



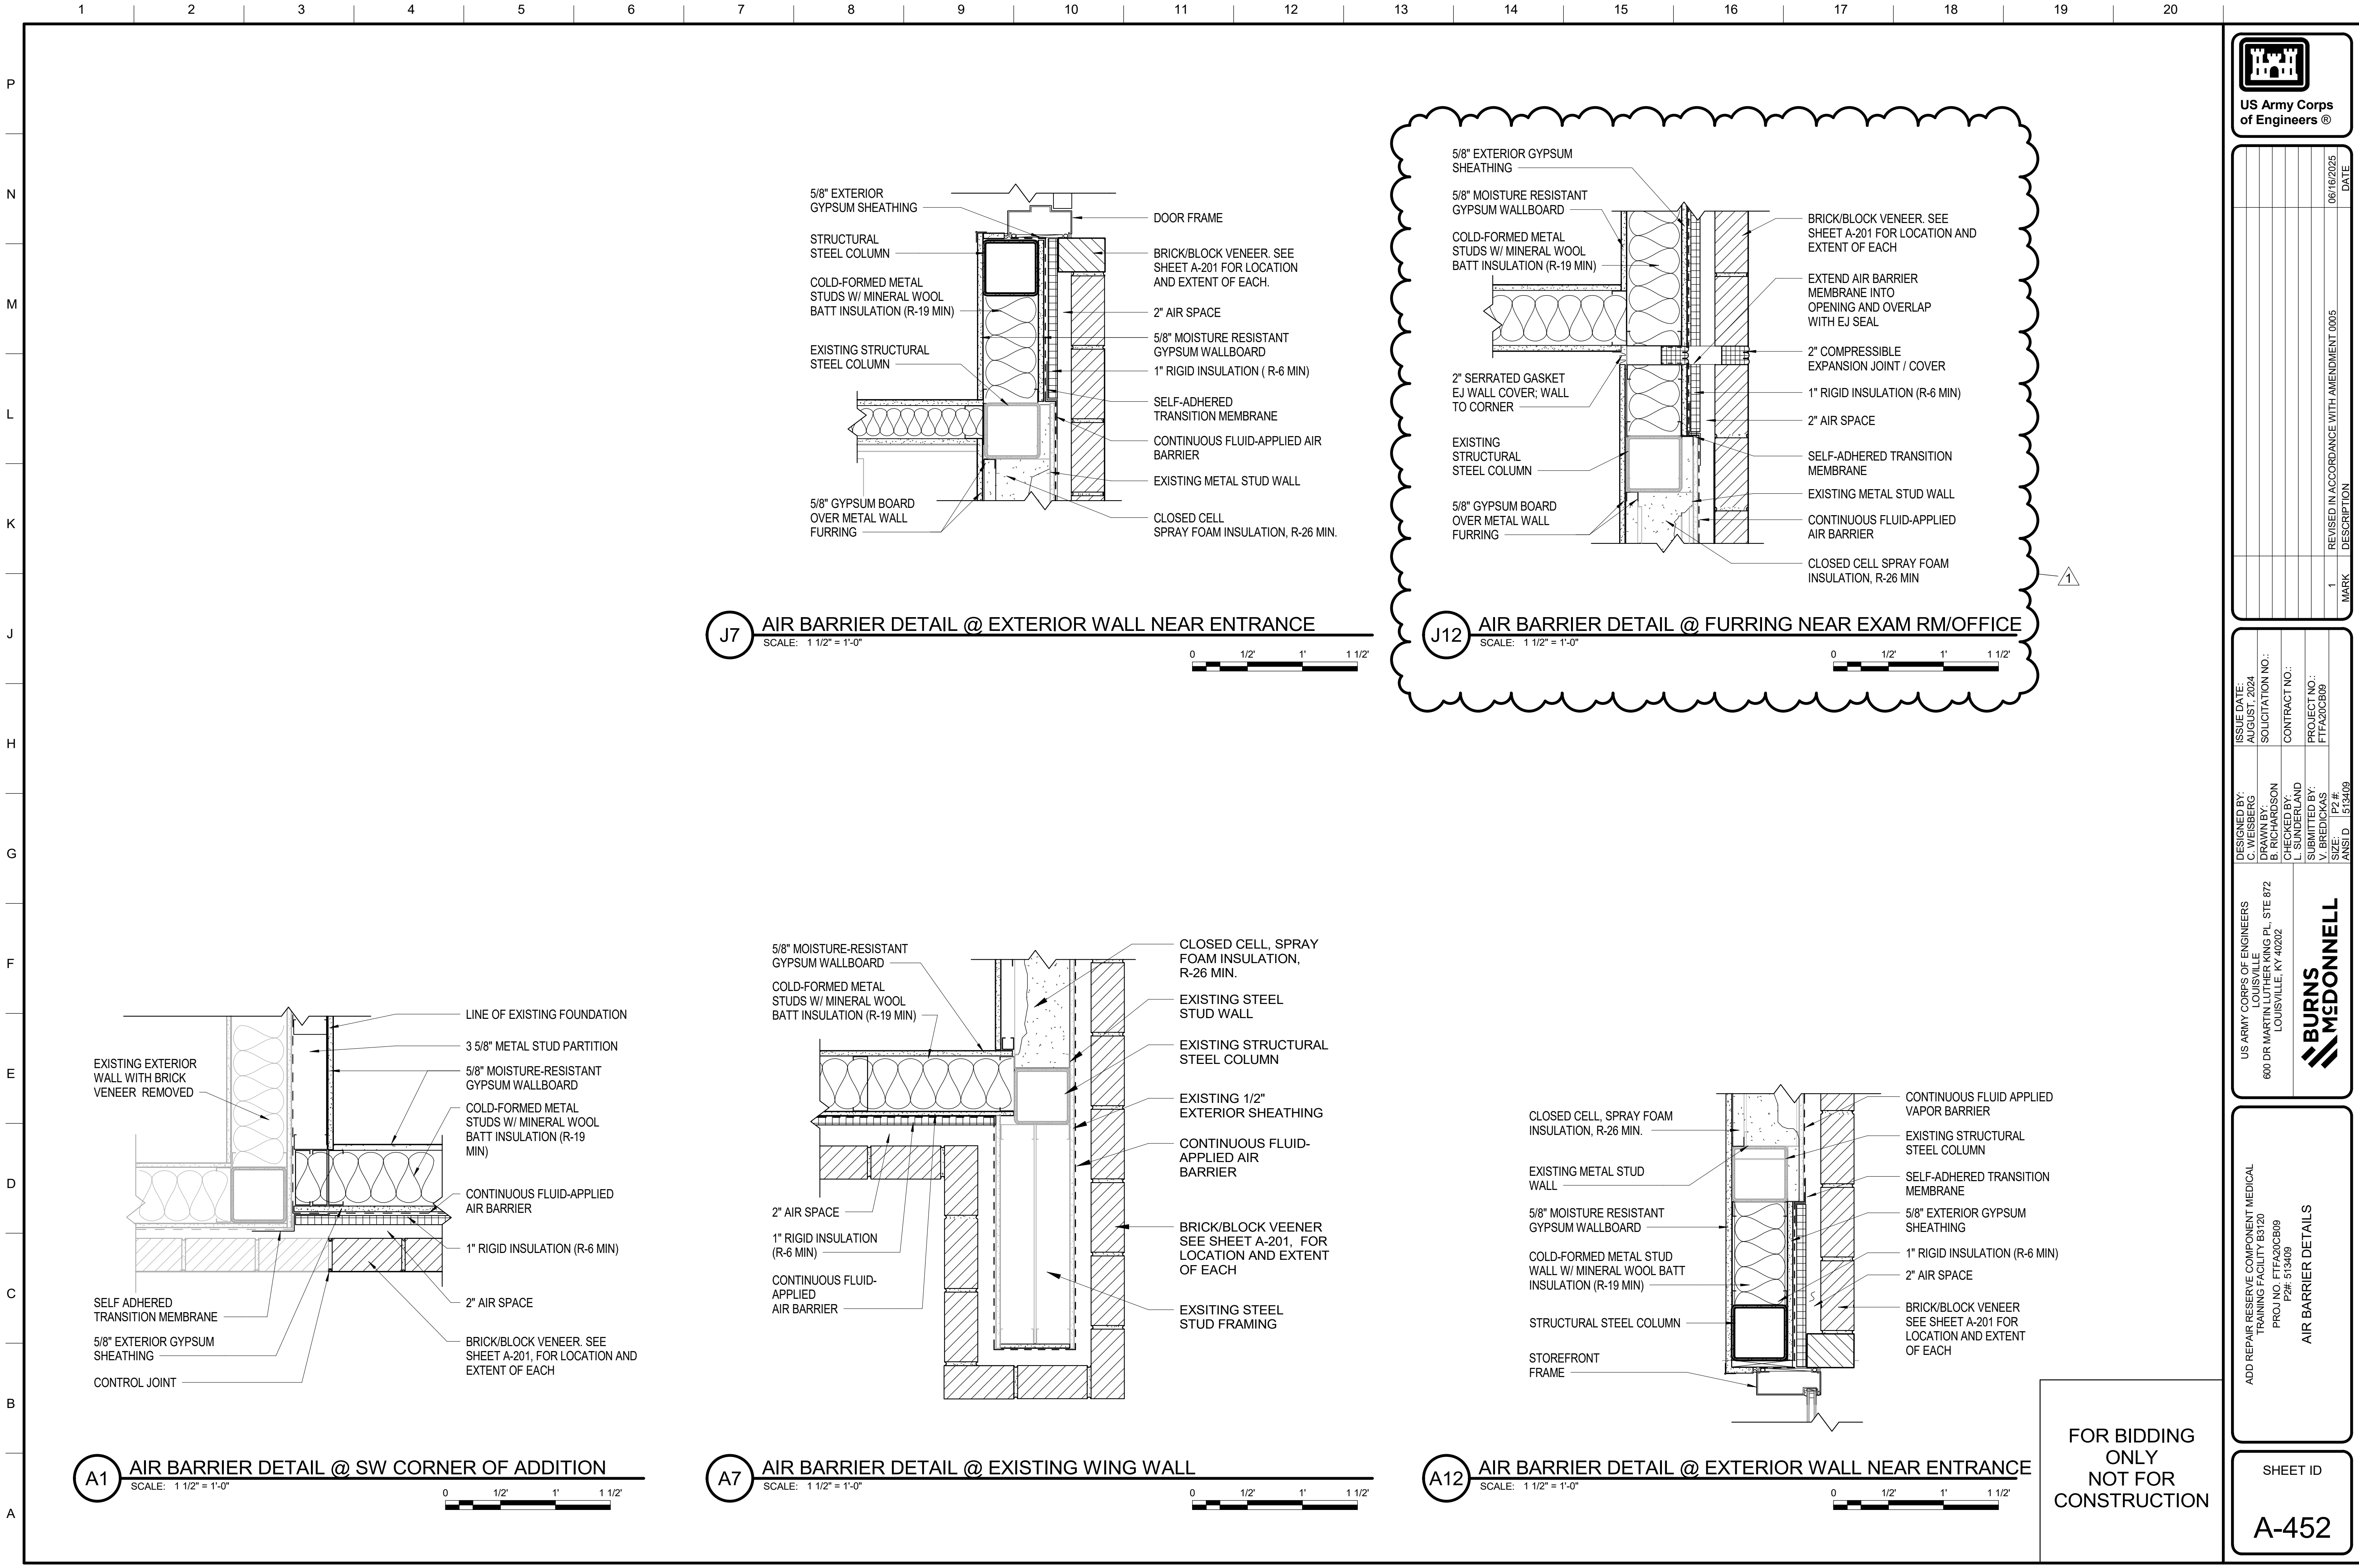

|                                |  |                            |                                          |      |
|--------------------------------|--|----------------------------|------------------------------------------|------|
| DESIGNED BY:<br>C. WEISBERG    |  | ISSUE DATE:<br>AUGUST 2024 | REVISN IN ACCORDANCE WITH AMENDMENT 0005 | DATE |
| DRAWN BY:<br>B. RICHARDSON     |  | SOLICITATION NO.:          |                                          |      |
| CHECKED BY:<br>L. SUNDERLAND   |  | CONTRACT NO.:              |                                          |      |
| SUBMITTED BY:<br>V. BREDDICKAS |  | PROJECT NO.:               |                                          |      |
| ANSI D 153409                  |  | SIZE: P2 #:                | 1                                        | MARK |


A-452



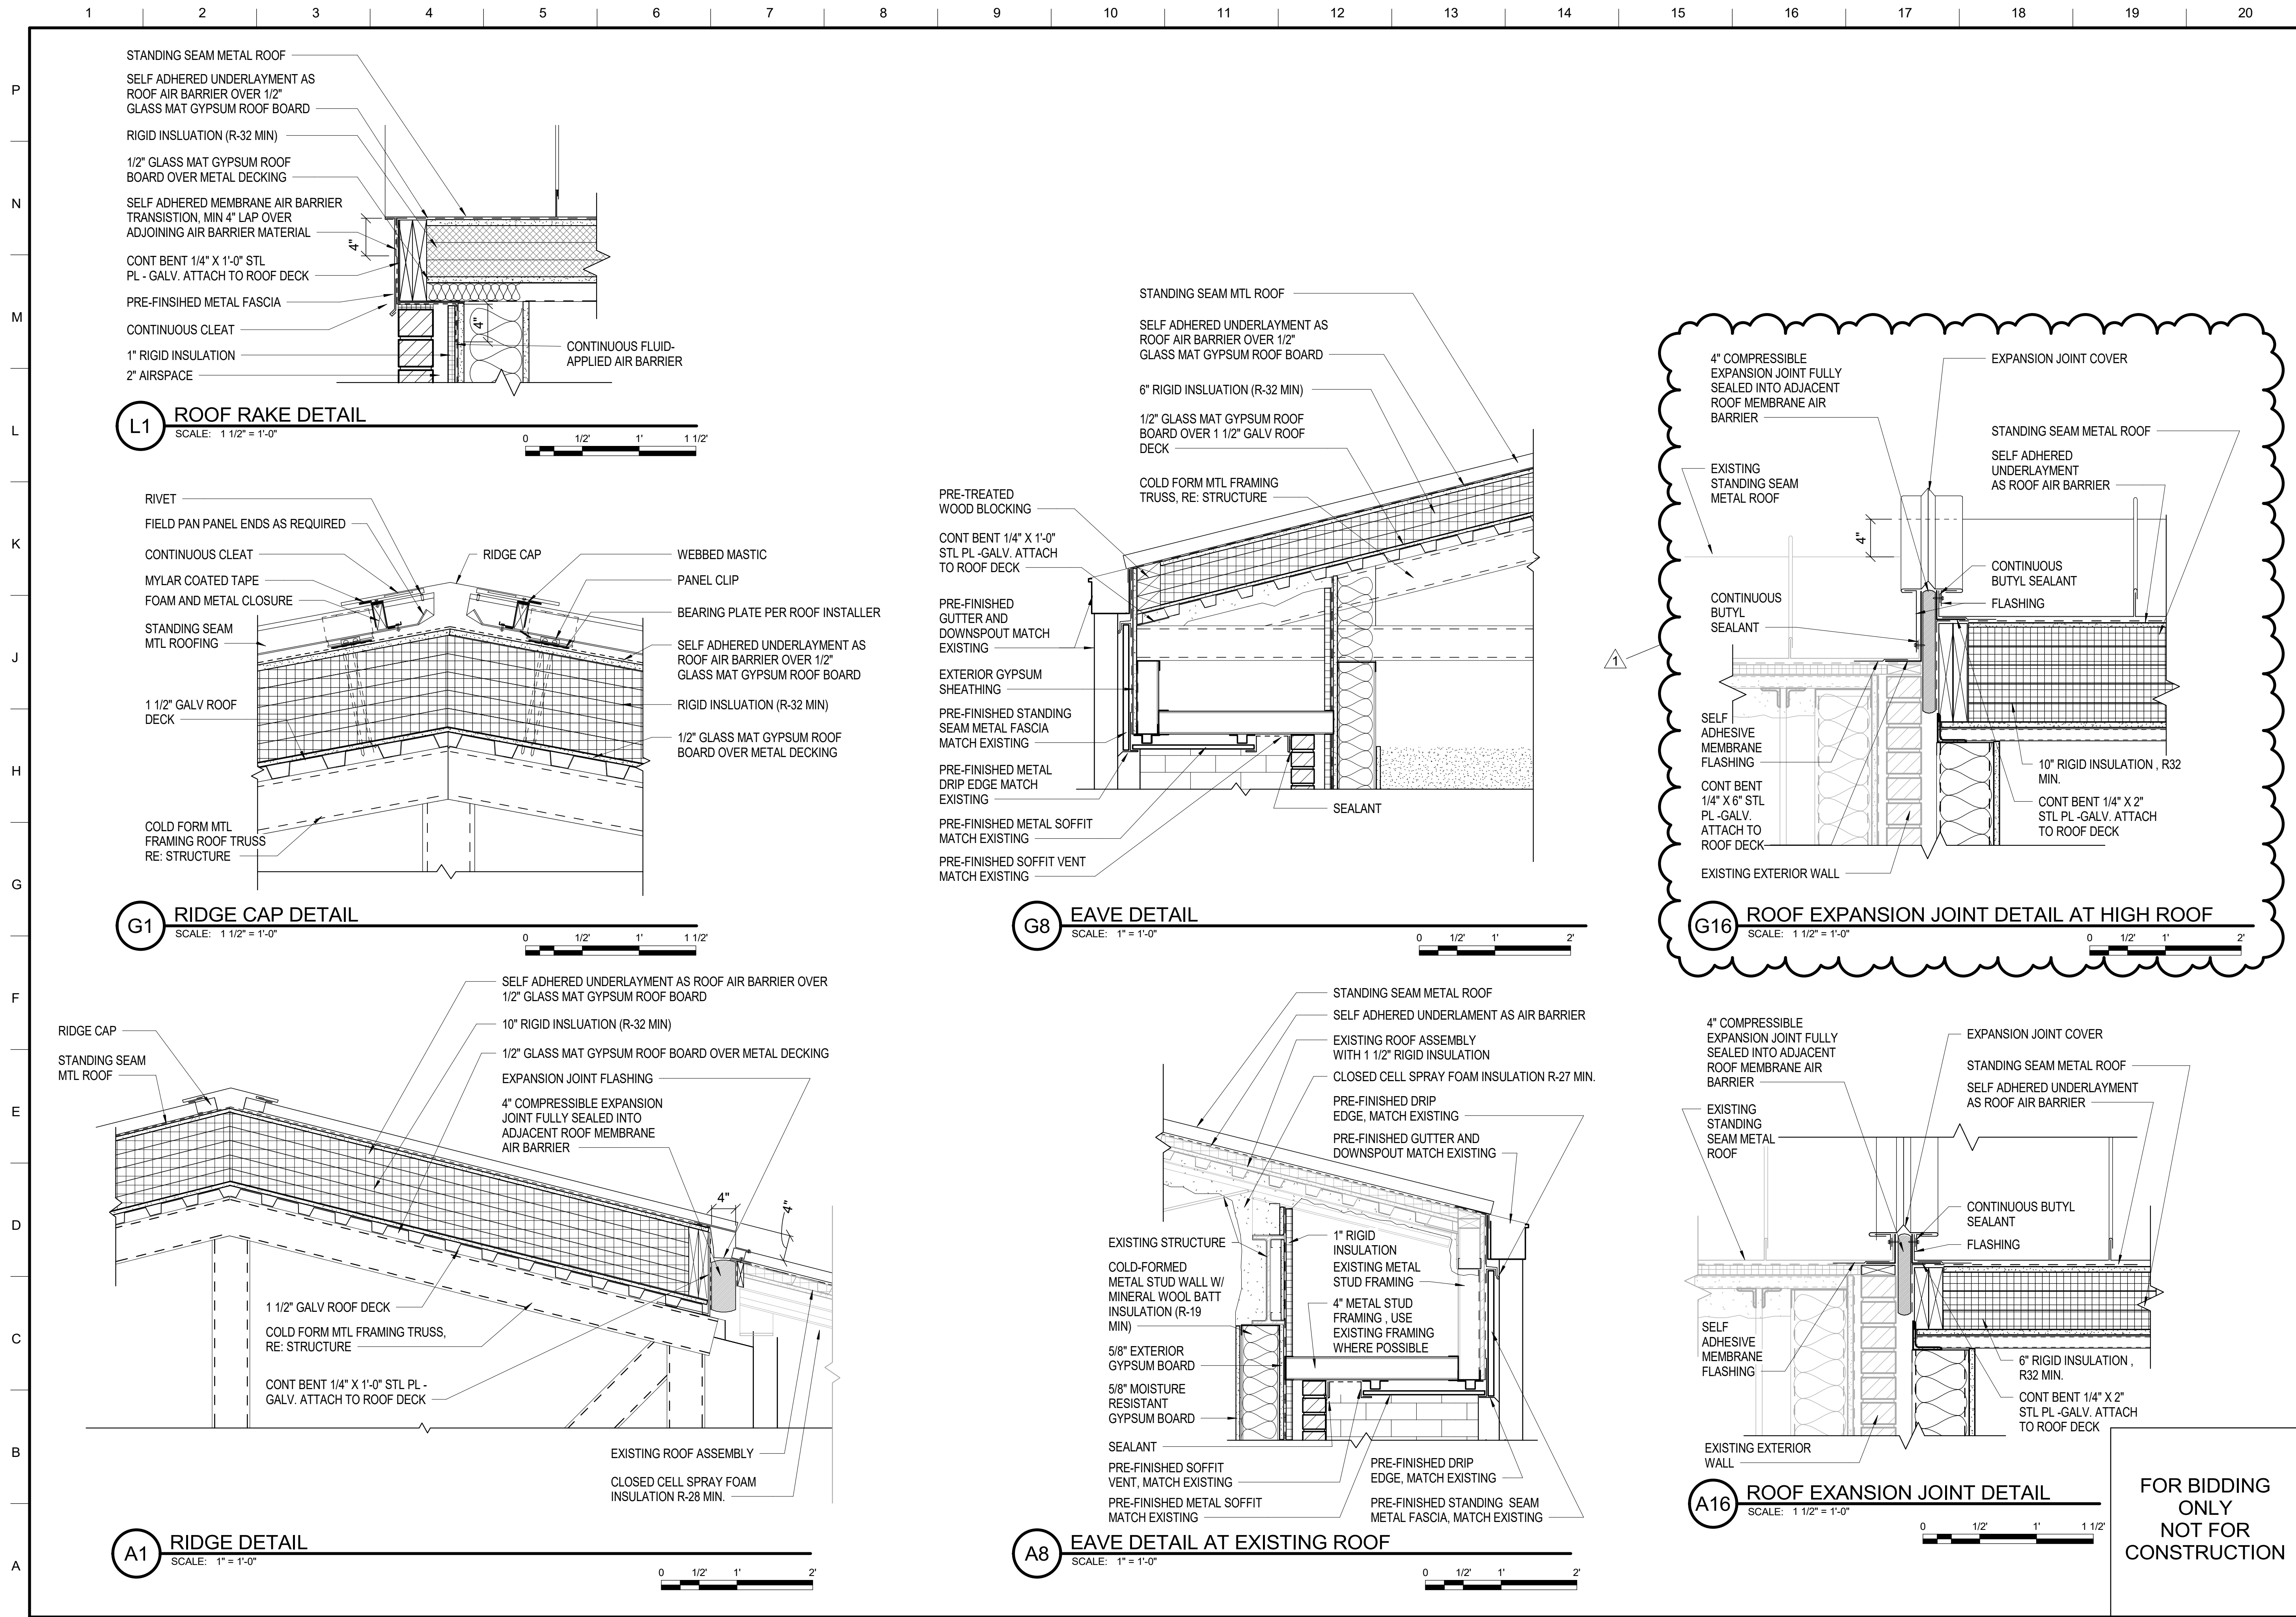

US Army Corps  
of Engineers®

|            |                                            |
|------------|--------------------------------------------|
| 09/16/2025 | DATE                                       |
| 1          | REVISION IN ACCORDANCE WITH AMENDMENT 0005 |
| 1          | DESCRIPTION                                |

|                                |                            |                   |
|--------------------------------|----------------------------|-------------------|
| DESIGNED BY:<br>C. WEISBERG    | ISSUE DATE:<br>AUGUST 2024 | SOLICITATION NO.: |
| DRAWN BY:<br>B. RICHARDSON     | CONTRACT NO.:              |                   |
| CHECKED BY:<br>L. SUNDERLAND   | PROJECT NO.:               |                   |
| SUBMITTED BY:<br>V. BREDDICKAS | FTFA20CB09                 |                   |
| SIZE:<br>P2 #:                 | ANSI D                     | 1513409           |

US ARMY CORPS OF ENGINEERS  
LOUISVILLE  
600 DR MARTIN LUTHER KING PL, STE 872  
LOUISVILLE, KY 40202

**BURNS  
& MCDONNELL**

ADD REPAIR RESERVE COMPONENT MEDICAL  
TRAINING FACILITY B3120  
PRCU NO. FTFA20CB09  
P2# 513409

ROOF DETAILS

SHEET ID


A-571

CORRECTED FINAL SUBMITTAL

W912QR-51061297 CORRFinal\_Plan-0005

FOR BIDDING  
ONLY  
NOT FOR  
CONSTRUCTION



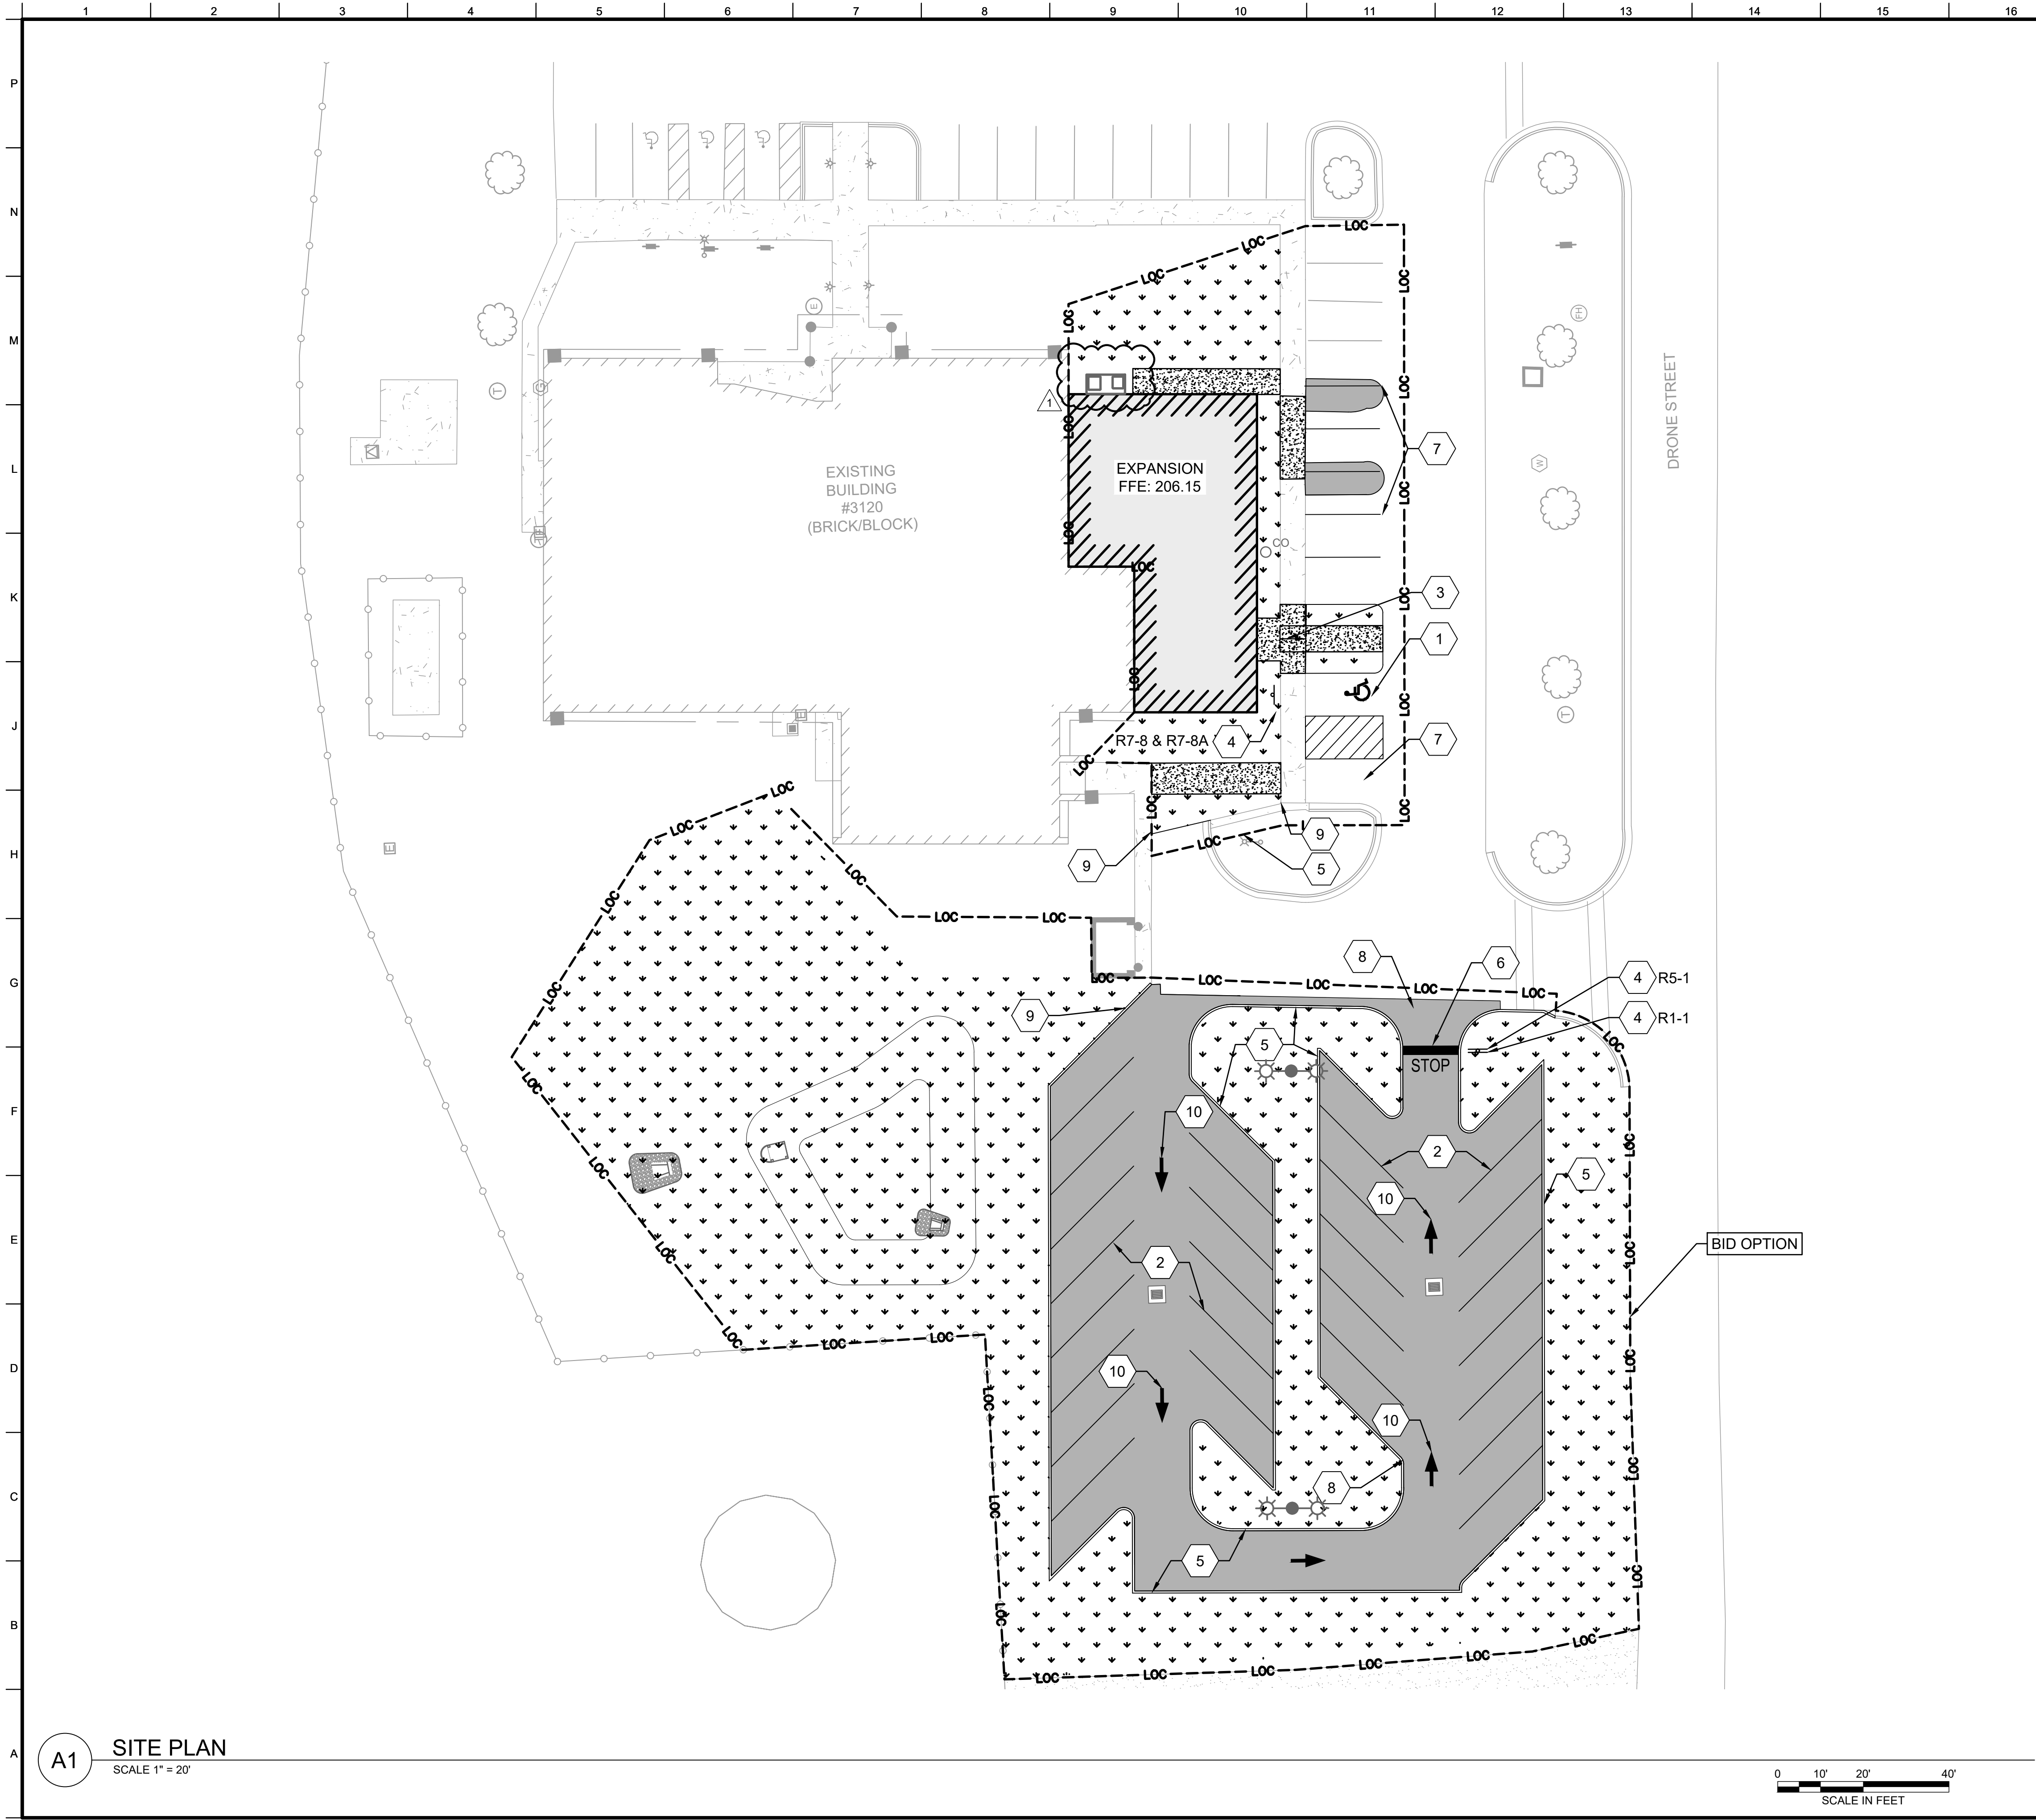


**A1** SITE PLAN  
SCALE 1" = 20'



FOR BIDDING  
ONLY  
NOT FOR  
CONSTRUCTION

**GENERAL SHEET NOTES**

- SEE SHEET C002 AND C003 FOR GENERAL SITE NOTES.
- EXISTING CONDITIONS SHOWN ARE COMPILED FROM SURVEY THAT WAS PERFORMED BY ATHENA ENGINEERING AND ENVIRONMENTAL, LLC IN OCTOBER, 2023.
- ALL TRAFFIC MARKINGS AND SIGNAGE MUST COMPLY WITH MUTCD LATEST EDITION.
- TOTAL NEW PARKING SPACES: 39
  - 38 STANDARD SPACES
  - 1 ACCESSIBLE SPACES

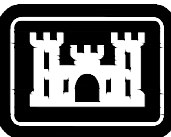

US Army Corps  
of Engineers®

| DATE        | 08/12/2025                                  |
|-------------|---------------------------------------------|
| DESCRIPTION | 1 REVISED IN ACCORDANCE WITH AMENDMENT 0005 |
| MARK        | 1                                           |

**SHEET KEYNOTES**

- |    |                                            |     |       |
|----|--------------------------------------------|-----|-------|
| 1  | ACCESSIBLE PARKING SPACE                   | A2  | CS502 |
| 2  | STANDARD 45° PARKING STALL                 | A9  | CS502 |
| 3  | ACCESSIBLE RAMP                            | K14 | CS501 |
| 4  | TYPICAL TRAFFIC SIGN INSTALLATION          | H12 | CS502 |
| 5  | HEADER CURB                                | F2  | CS501 |
| 6  | PAINTED STOP BAR                           | A14 | CS502 |
| 7  | STANDARD 90° PARKING STALL                 | H7  | CS502 |
| 8  | AC - AC TRANSITION                         | F14 | CS501 |
| 9  | HEADER CURB TAPER END                      | F2  | CS501 |
| 10 | PAINTED TRAFFIC ARROW (FDOT INDEX 711-001) |     |       |
| 11 | MECHANICAL EQUIPMENT                       |     |       |

**LEGEND**

- |  |                   |    |       |
|--|-------------------|----|-------|
|  | BUILDING          |    |       |
|  | ASPHALT PAVEMENT  | A2 | CS501 |
|  | CONCRETE SIDEWALK | A8 | CS501 |
|  | SOD               |    |       |

|                               |                             |
|-------------------------------|-----------------------------|
| DESIGNED BY:<br>B. TSUI       | ISSUE DATE:<br>AUGUST, 2024 |
| DRAWN BY:<br>B. TSUI          | SOLICITATION NO.:           |
| CHECKED BY:<br>M. PAREDES     | CONTRACT NO.:               |
| SUBMITTED BY:<br>V. BREDICKAS | PROJECT NO.:                |
| SIZE:<br>P2 # 513409          | ANSI D 513409               |


U.S. ARMY CORPS OF ENGINEERS  
LOUISVILLE DISTRICT  
600 DR MARTIN LUTHER KING PL, STE 872  
LOUISVILLE, KY 40202

**BURNS MEDONNELL**

|   |           |
|---|-----------|
| ADDITION REPAIR COMPONENT MEDICAL<br>TRAINING FACILITY B3120<br>PROJ NO. FTFA20CB09<br>PZ#: 513409 | SITE PLAN |
|---|-----------|

|          |       |
|----------|-------|
| SHEET ID | CS100 |
|----------|-------|



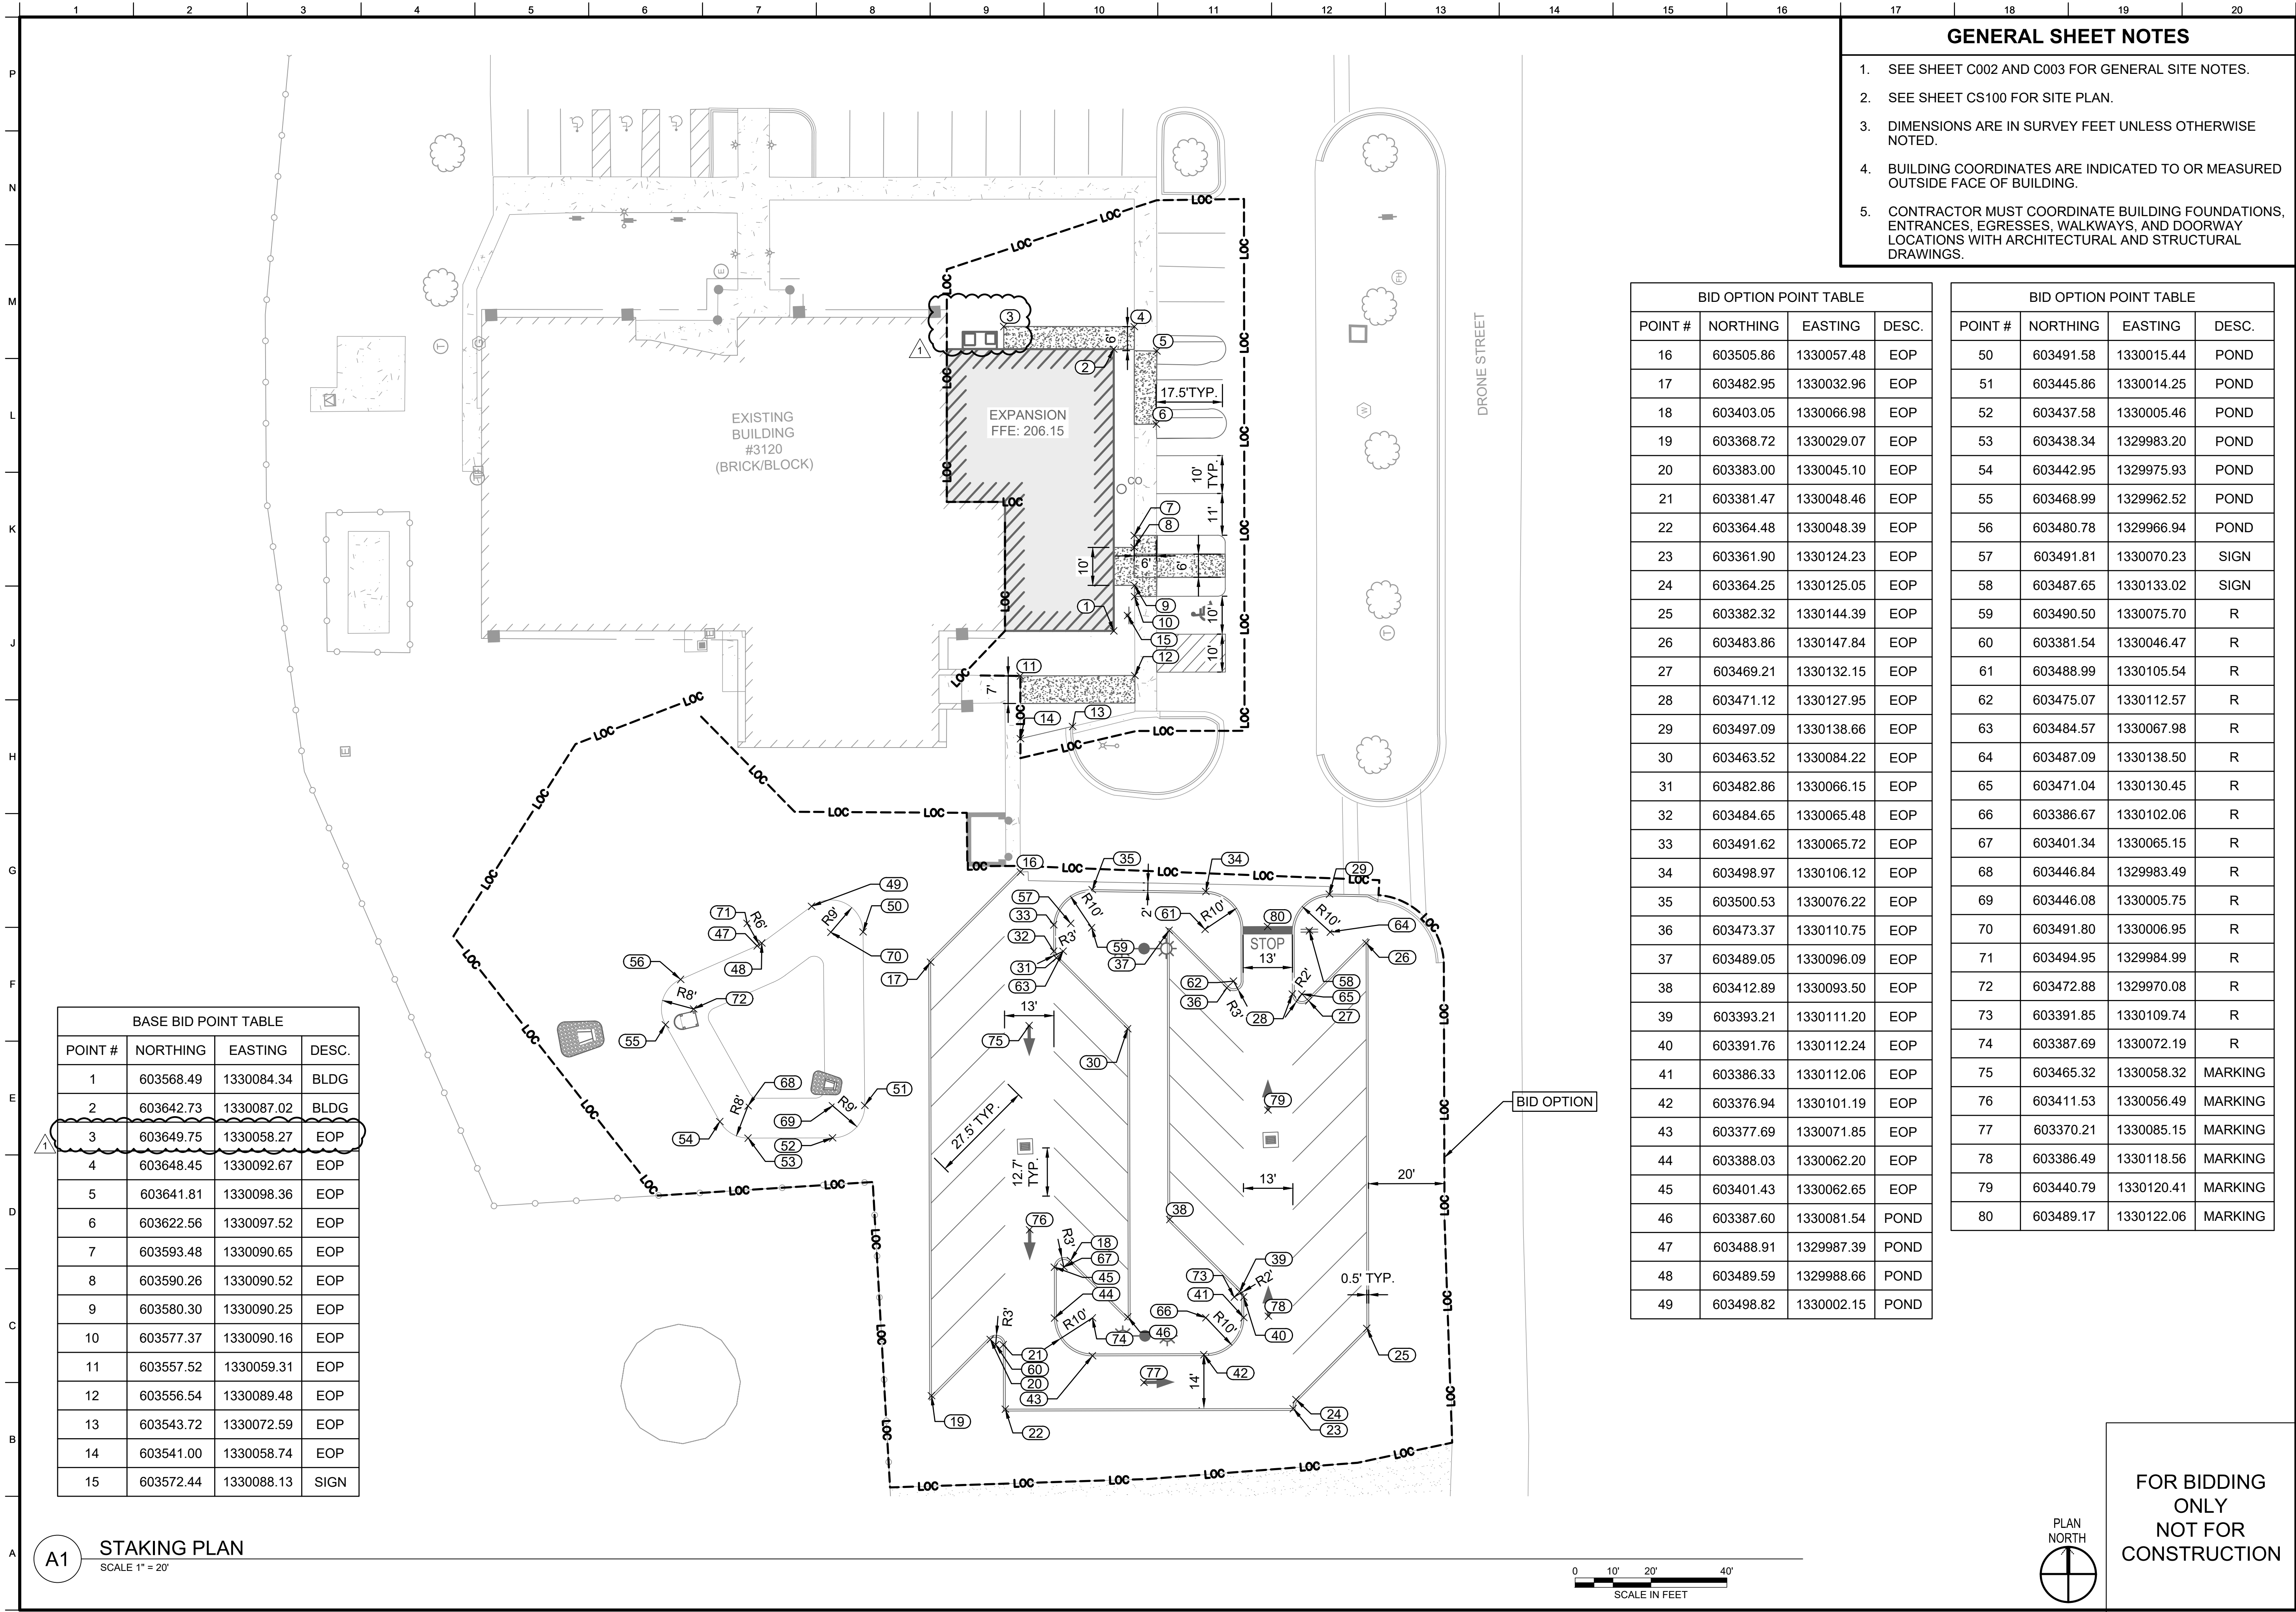

| BASE BID POINT TABLE |           |            |       |
|----------------------|-----------|------------|-------|
| POINT #              | NORTHING  | EASTING    | DESC. |
| 1                    | 603568.49 | 1330084.34 | BLDG  |
| 2                    | 603642.73 | 1330087.02 | BLDG  |
| 3                    | 603649.75 | 1330058.27 | EOP   |
| 4                    | 603648.45 | 1330092.67 | EOP   |
| 5                    | 603641.81 | 1330098.36 | EOP   |
| 6                    | 603622.56 | 1330097.52 | EOP   |
| 7                    | 603593.48 | 1330090.65 | EOP   |
| 8                    | 603590.26 | 1330090.52 | EOP   |
| 9                    | 603580.30 | 1330090.25 | EOP   |
| 10                   | 603577.37 | 1330090.16 | EOP   |
| 11                   | 603557.52 | 1330059.31 | EOP   |
| 12                   | 603556.54 | 1330089.48 | EOP   |
| 13                   | 603543.72 | 1330072.59 | EOP   |
| 14                   | 603541.00 | 1330058.74 | EOP   |
| 15                   | 603572.44 | 1330088.13 | SIGN  |

- GENERAL SHEET NOTES
1.

SEE SHEET C002 AND C003 FOR GENERAL SITE NOTES.
2.

SEE SHEET CS100 FOR SITE PLAN.
3.

DIMENSIONS ARE IN SURVEY FEET UNLESS OTHERWISE NOTED.
4.

BUILDING COORDINATES ARE INDICATED TO OR MEASURED OUTSIDE FACE OF BUILDING.
5.

CONTRACTOR MUST COORDINATE BUILDING FOUNDATIONS, ENTRANCES, EGRESS, WALKWAYS, AND DOORWAY LOCATIONS WITH ARCHITECTURAL AND STRUCTURAL DRAWINGS.

| BID OPTION POINT TABLE |           |            |       |
|------------------------|-----------|------------|-------|
| POINT #                | NORTHING  | EASTING    | DESC. |
| 16                     | 603505.86 | 1330057.48 | EOP   |
| 17                     | 603482.95 | 1330032.96 | EOP   |
| 18                     | 603403.05 | 1330066.98 | EOP   |
| 19                     | 603368.72 | 1330029.07 | EOP   |
| 20                     | 603383.00 | 1330045.10 | EOP   |
| 21                     | 603381.47 | 1330048.46 | EOP   |
| 22                     | 603364.48 | 1330048.39 | EOP   |
| 23                     | 603361.90 | 1330124.23 | EOP   |
| 24                     | 603364.25 | 1330125.05 | EOP   |
| 25                     | 603382.32 | 1330144.39 | EOP   |
| 26                     | 603483.86 | 1330147.84 | EOP   |
| 27                     | 603469.21 | 1330132.15 | EOP   |
| 28                     | 603471.12 | 1330127.95 | EOP   |
| 29                     | 603497.09 | 1330138.66 | EOP   |
| 30                     | 603463.52 | 1330084.22 | EOP   |
| 31                     | 603482.86 | 1330066.15 | EOP   |
| 32                     | 603484.65 | 1330065.48 | EOP   |
| 33                     | 603491.62 | 1330065.72 | EOP   |
| 34                     | 603498.97 | 1330106.12 | EOP   |
| 35                     | 603500.53 | 1330076.22 | EOP   |
| 36                     | 603473.37 | 1330110.75 | EOP   |
| 37                     | 603489.05 | 1330096.09 | EOP   |
| 38                     | 603412.89 | 1330093.50 | EOP   |
| 39                     | 603393.21 | 1330111.20 | EOP   |
| 40                     | 603391.76 | 1330112.24 | EOP   |
| 41                     | 603386.33 | 1330112.06 | EOP   |
| 42                     | 603376.94 | 1330101.19 | EOP   |
| 43                     | 603377.69 | 1330071.85 | EOP   |
| 44                     | 603388.03 | 1330062.20 | EOP   |
| 45                     | 603401.43 | 1330062.65 | EOP   |
| 46                     | 603387.60 | 1330081.54 | POND  |
| 47                     | 603488.91 | 1329987.39 | POND  |
| 48                     | 603489.59 | 1329988.66 | POND  |
| 49                     | 603498.82 | 1330002.15 | POND  |

| BID OPTION POINT TABLE |           |            |         |
|------------------------|-----------|------------|---------|
| POINT #                | NORTHING  | EASTING    | DESC.   |
| 50                     | 603491.58 | 1330015.44 | POND    |
| 51                     | 603445.86 | 1330014.25 | POND    |
| 52                     | 603437.58 | 1330005.46 | POND    |
| 53                     | 603438.34 | 1329983.20 | POND    |
| 54                     | 603442.95 | 1329975.93 | POND    |
| 55                     | 603468.99 | 1329962.52 | POND    |
| 56                     | 603480.78 | 1329966.94 | POND    |
| 57                     | 603491.81 | 1330070.23 | SIGN    |
| 58                     | 603487.65 | 1330133.02 | SIGN    |
| 59                     | 603490.50 | 1330075.70 | R       |
| 60                     | 603381.54 | 1330046.47 | R       |
| 61                     | 603488.99 | 1330105.54 | R       |
| 62                     | 603475.07 | 1330112.57 | R       |
| 63                     | 603484.57 | 1330067.98 | R       |
| 64                     | 603487.09 | 1330138.50 | R       |
| 65                     | 603471.04 | 1330130.45 | R       |
| 66                     | 603386.67 | 1330102.06 | R       |
| 67                     | 603401.34 | 1330065.15 | R       |
| 68                     | 603446.84 | 1329983.49 | R       |
| 69                     | 603446.08 | 1330005.75 | R       |
| 70                     | 603491.80 | 1330006.95 | R       |
| 71                     | 603494.95 | 1329984.99 | R       |
| 72                     | 603472.88 | 1329970.08 | R       |
| 73                     | 603391.85 | 1330109.74 | R       |
| 74                     | 603387.69 | 1330072.19 | R       |
| 75                     | 603465.32 | 1330058.32 | MARKING |
| 76                     | 603411.53 | 1330056.49 | MARKING |
| 77                     | 603370.21 | 1330085.15 | MARKING |
| 78                     | 603386.49 | 1330118.56 | MARKING |
| 79                     | 603440.79 | 1330120.41 | MARKING |
| 80                     | 603489.17 | 1330122.06 | MARKING |

A1

STAKING PLAN

SCALE 1" = 20'



FOR BIDDING  
ONLY  
NOT FOR  
CONSTRUCTION

US Army Corps  
of Engineers®

ISSUE DATE:  
AUGUST 2024

DESIGNED BY:  
B. TSUI

CHECKED BY:  
M. PAREDES

SUBMITTED BY:  
V. BREDICKAS

SIZE:  
ANSI D

SOLICITATION NO.:  
600 DR MARTIN LUTHER KING PL STE 872  
LOUISVILLE, KY 40202

CONTRACT NO.:  
FTFA20CB09

PROJECT NO.:  
FTFA20CB09

P2 #:  
513409

ADDITON REPAIR COMPONENT MEDICAL  
TRAINING FACILITY B3120  
PROJ. NO. FTFA20CB09  
P2# 513409

STAKING PLAN

SHEET ID

CS110

1

REVISD IN ACCORDANCE WITH AMENDMENT 0005

MARK

DESCRIPTION

08/12/2025

DATE


9/12/2025 3:45:11 PM

z:\Clients\ANFL\BSC\ELL11153466\_gim\mat33120\Design\CS110\Sheet\CS110.dwg

W912QR-51061297 CORRFinal\_Plans-0005

CORRECTED FINAL SUBMITTAL



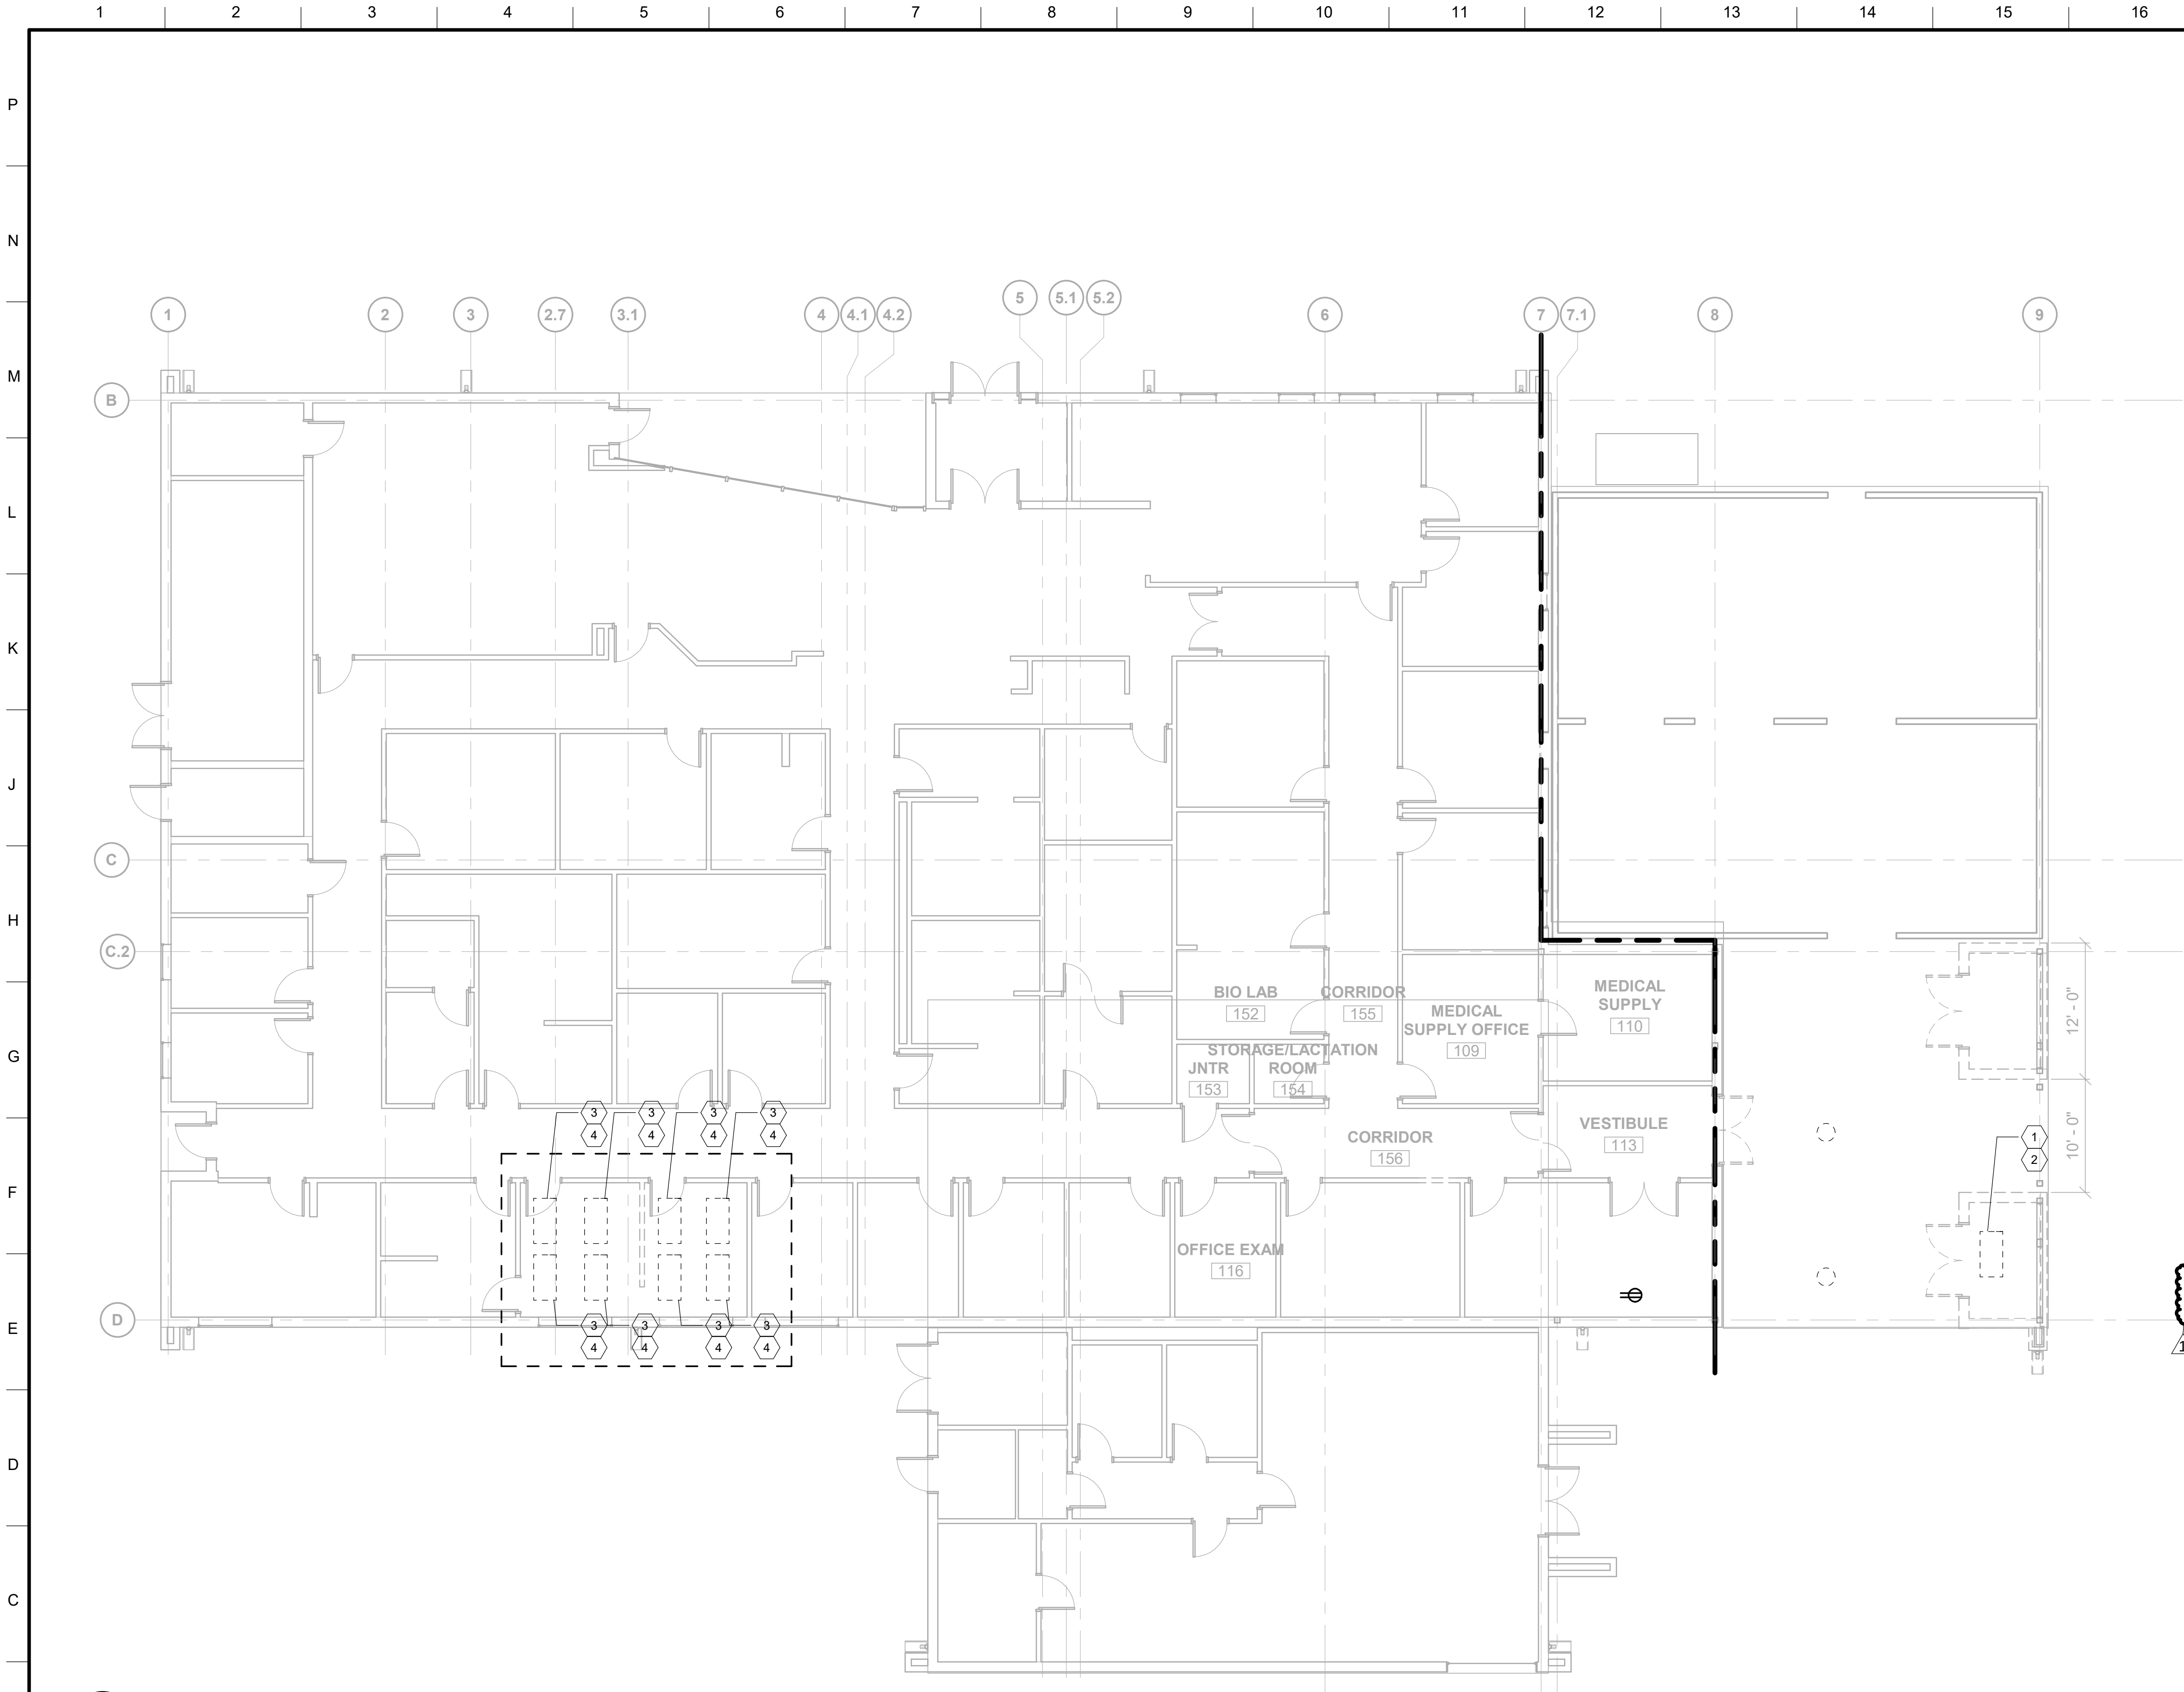

**B1** LEVEL 1 - ELECTRICAL DEMOLITION  
SCALE: 1/8" = 1'-0"

## GENERAL SHEET NOTES

- SEE CIVIL DEMO SHEET FOR FURTHER DEMOLITION ITEMS AND SEE E-001 FOR ELECTRICAL GENERAL NOTES, LEGEND AND ABBREVIATIONS.
- ABANDON CONDUITS IN PLACE DURING ELECTRICAL DEMOLITION.
- THE LOCATION OF EXISTING UTILITIES IS APPROXIMATE. THE CONTRACTOR MUST CONFIRM THE LOCATION OF EXISTING UTILITIES PRIOR TO COMMENCING EXCAVATION.
- ALL EXISTING RACEWAYS, FEEDERS, ELECTRICAL DISTRIBUTION EQUIPMENT AND DEVICES ARE NOT SHOWN IN THESE DOCUMENTS. IT IS THE RESPONSIBILITY OF THE ELECTRICAL CONTRACTOR TO INSPECT THE EXISTING CONDITIONS AND IDENTIFY ALL ELECTRICAL ITEMS OUTSIDE THE SCOPE OF WORK AREA AND THAT ARE AFFECTED AS A RESULT OF THE NEW WORK. THE ELECTRICAL CONTRACTOR MUST ALSO CARRY AN ALLOWANCE FOR UNFORESEEN FIELD CONDITIONS THAT MIGHT RESULT IN OFFSETS AND RELOCATIONS OF ELECTRICAL EQUIPMENT. THE ELECTRICAL CONTRACTOR MUST NOTIFY THE DESIGN TEAM AND THE OWNER OF ANY UNFORESEEN CONDITIONS NOT IDENTIFIED IN THESE DOCUMENTS PRIOR TO COMMENCING WORK.
- IF DISCREPANCIES ARE FOUND BETWEEN PLANS AND EXISTING CONDITIONS AT SITE, THE CONTRACTOR MUST CONTACT ENGINEER PRIOR TO PERFORMING WORK.
- AT DEMOLITION STAGE, ELECTRICAL CONTRACTOR WILL BERESPONSIBLE FOR IDENTIFYING TAGGING OUT AND LOCKING OUTALL AFFECTED CIRCUITS PRIOR TO START OF DEMOLITION.
- CONTRACTOR MUST COORDINATE THE WORK BEFORE DEMOLITION TO AVOID DAMAGE OR REMOVAL OF FIXTURES NOTRELATED TO THIS PROJECT.
- THE CONTRACTOR MUST MAINTAIN CONTINUITY OF CIRCUITSWHERE EXISTING EQUIPMENT IS TO BE REMOVED AND DOWN STREAM DEVICES MAY BE EFFECTED.
- THE CONTRACTOR MUST EXERCISE CARE SO THAT ONLY THAT CONSTRUCTION INDICATED OR REASONABLY IMPLIED TO BE REMOVED MUST BE DEMOLISHED. THE EXISTING CONSTRUCTIONTO REMAIN MUST BE LEFT INTACT AND UNDAMAGED. THE ONTRACTOR MUST PROTECT ALL ADJACENT SURFACES AND ATERIALS AS REQUIRED TO PREVENT DAMAGE.
- THE CONTRACTOR MUST COORDINATE ALL POWER INTERRUPTIONS WITH THE OWNER.

## SHEET KEYNOTES

- REMOVE ALL LIGHTING FIXTURE IN THIS AREA AND RETURN TO OWNER.
- REMOVE ALL RACEWAYS AND CABLES BACK TO SOURCE.
- DISCONNECT AND REMOVE ALL LIGHT FIXTURES AND RETURN TO OWNER.
- DISCONNECT LIGHTING CIRCUITS AND MAKE SAFE TO REUSE IN NEW WORK DURING LIGHTING RECONNECTION.



US Army Corps  
of Engineers®

| DATE        | 06/19/2025                                |
|-------------|-------------------------------------------|
| DESCRIPTION | REVISED IN ACCORDANCE WITH AMENDMENT 0005 |
| MARK        | 1                                         |

| DESIGNED BY:  | N. PEREZ                | ISSUE DATE:       | AUGUST 2024 |
|---------------|-------------------------|-------------------|-------------|
| DRAWN BY:     | N. HOAFU                | SOLICITATION NO.: |             |
| CHECKED BY:   | T. MORGAN               | CONTRACT NO.:     |             |
| SUBMITTED BY: | V. BREDICKAS            | PROJECT NO.:      | FTFA20CB09  |
| SIZE:         | P2 #:<br>ANSI D 1513409 |                   |             |


US ARMY CORPS OF ENGINEERS  
LOUISVILLE  
600 DR MARTIN LUTHER KING PL, STE 872  
LOUISVILLE, KY 40202

**BURNS  
MEDONNELL**

|   |
|---|
| ADD REPAIR RESERVE COMPONENT MEDICAL<br>TRAINING FACILITY B3120<br>PROJ NO. FTFA20CB09<br>P2# 513409<br>ELECTRICAL DEMOLITION |
|---|

|          |
|----------|
| SHEET ID |
| ED101    |

PLAN NORTH

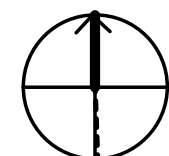

FOR BIDDING  
ONLY  
NOT FOR  
CONSTRUCTION