




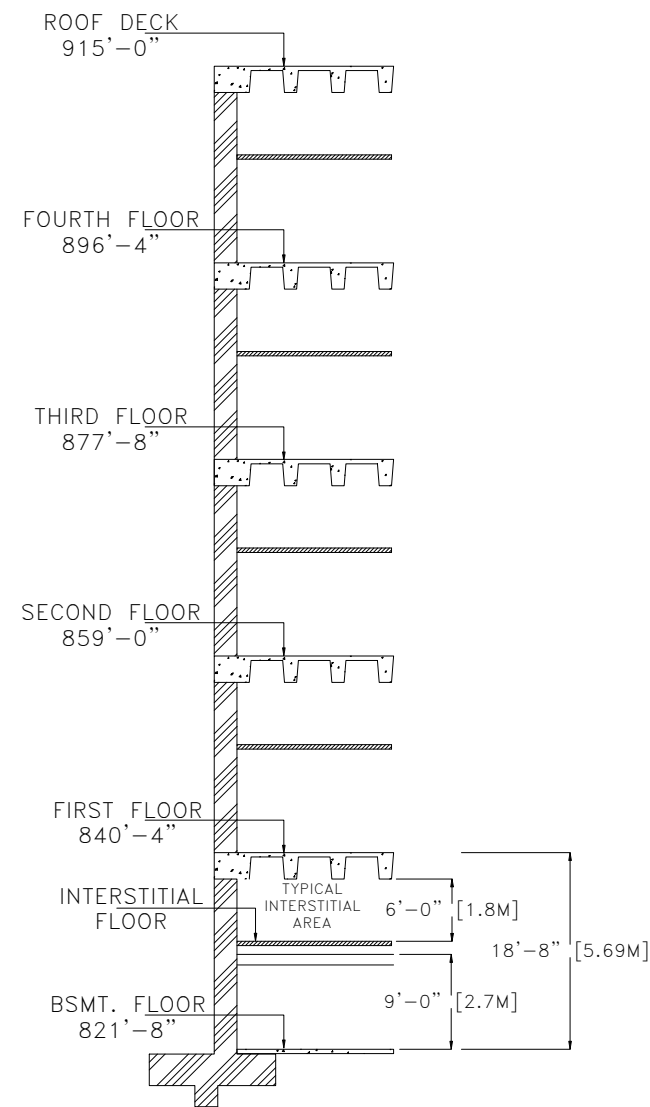

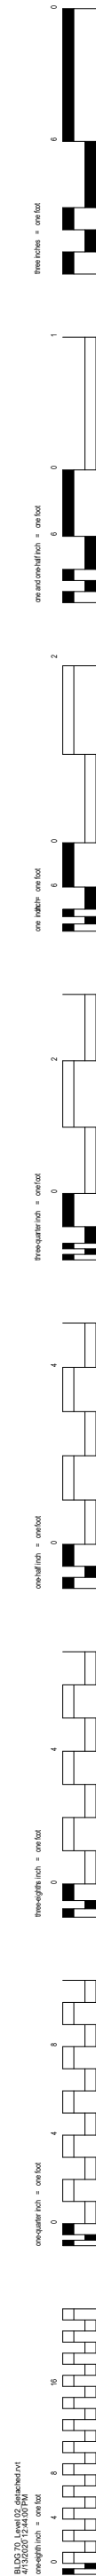

TYPICAL ELEVATION
NOT TO SCALE

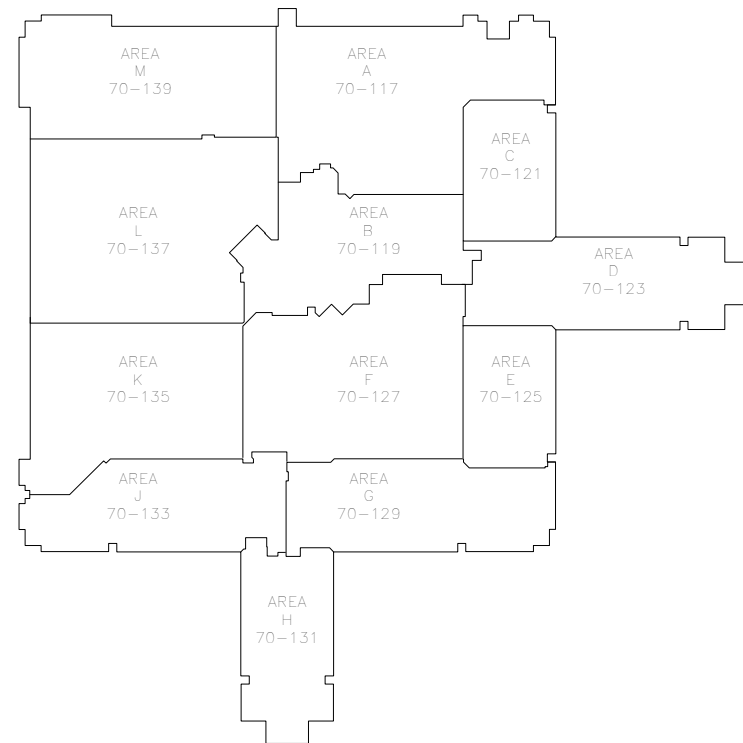

Critical Power (duplex)

Critical Power (Quad)

Telecom Room

Add Data Drop at
back wall of
Nurse-Station behind
the Display Boards

Pull from TR 2H-112

Each headwall to
receive duplex critical
power and Data Drop

Pull from TR 2H-112


LEVEL 2
1/32" = 1'-0"

REVISIONS	DATE

GENERAL
NOTES:

GENERAL CONTRACTOR AND/OR ALL SUBCONTRACTORS SHALL FIELD VERIFY ALL DIMENSIONS SHOWN ON THESE PLANS AND SHALL BE RESPONSIBLE FOR VARIATIONS BETWEEN PLAN DIMENSIONS AND ACTUAL FIELD DIMENSIONS. WHERE VARIATIONS ARE FOUND TO OCCUR, THE CONTRACTOR SHALL NOTIFY THE PROJECT ENGINEER IN WRITING PRIOR TO PROCEEDING WITH CONSTRUCTION. NO ADJUSTMENT TO THE WORK WILL BE MADE WITHOUT THE PRIOR APPROVAL OF THE PROJECT ENGINEER.

GENERAL CONTRACTOR SHALL BE RESPONSIBLE FOR GENERAL DEMOLITION INCLUDING REMOVAL OF WALLS, PARTITIONS, DOORS & CEILING & FLOORS. ANY AND ALL CUTTING OF CONCRETE FLOORS, WALLS OR STRUCTURE SHALL BE THE GENERAL CONTRACTORS RESPONSIBILITY. CORE DRILLING THROUGH CONCRETE FLOORS, WALLS OR STRUCTURE FOR PIPING OR CONDUIT SHALL BE THE RESPONSIBILITY OF THE SUBCONTRACTOR BY TRADE. PRESTOPPING OF THESE OPENINGS SHALL BE DONE BY THE RESPECTIVE SUBCONTRACTOR. REMOVAL OF DEBRIS RESULTING FROM DEMOLITION, CUTTING, AND/OR DRILLING IS THE RESPONSIBILITY OF THE GENERAL CONTRACTOR. PATCHING AND REPAIR OF CONCRETE WALLS, FLOOR, OR STRUCTURE SHALL BE THE RESPONSIBILITY OF THE GENERAL CONTRACTOR. THIS WILL BE ACCOMPLISHED UPON COMPLETION OF THE INSTALLATION OF ANY AND ALL UTILITIES INSTALLED BY THE VARIOUS SUBCONTRACTORS.

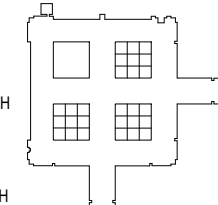

I HEREBY CERTIFY THAT THIS PLAN, SPECIFICATION, OR OTHER DOCUMENT IS A TRUE AND CORRECT REPRESENTATION OF THE DESIGN AND CONSTRUCTION OF THE PROJECT AND THAT I AM A DULY LICENSED PROFESSIONAL ENGINEER UNDER THE LAWS OF THE STATE OF MINNESOTA.

REGISTRATION NUMBER: _____

Drawing Scale: 1/32" = 1'-0"

Plot Scale: _____

Drawing Title
2nd Floor Composite Plan

Approved: Division Chief _____

Approved: Service Director _____

Project Title
Minneapolis Veterans Health Administration

Location: Enter address here _____

Date: 1/30/2017

Checked: _____

Drawn: MJH

Project No.
140583


Building Number
70

DRAWING NO.
0000 - 002



Project Status 1/30/2017

Office of
Facilities
Management

Department of
Veterans Affairs

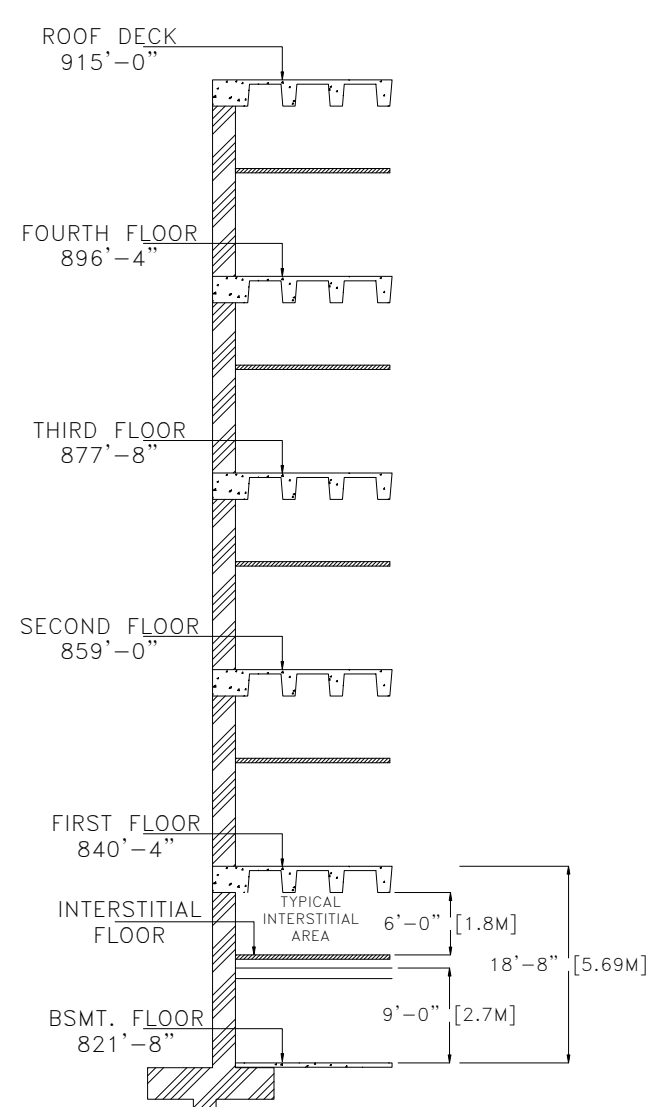


TYPICAL ELEVATION
NOT TO SCALE

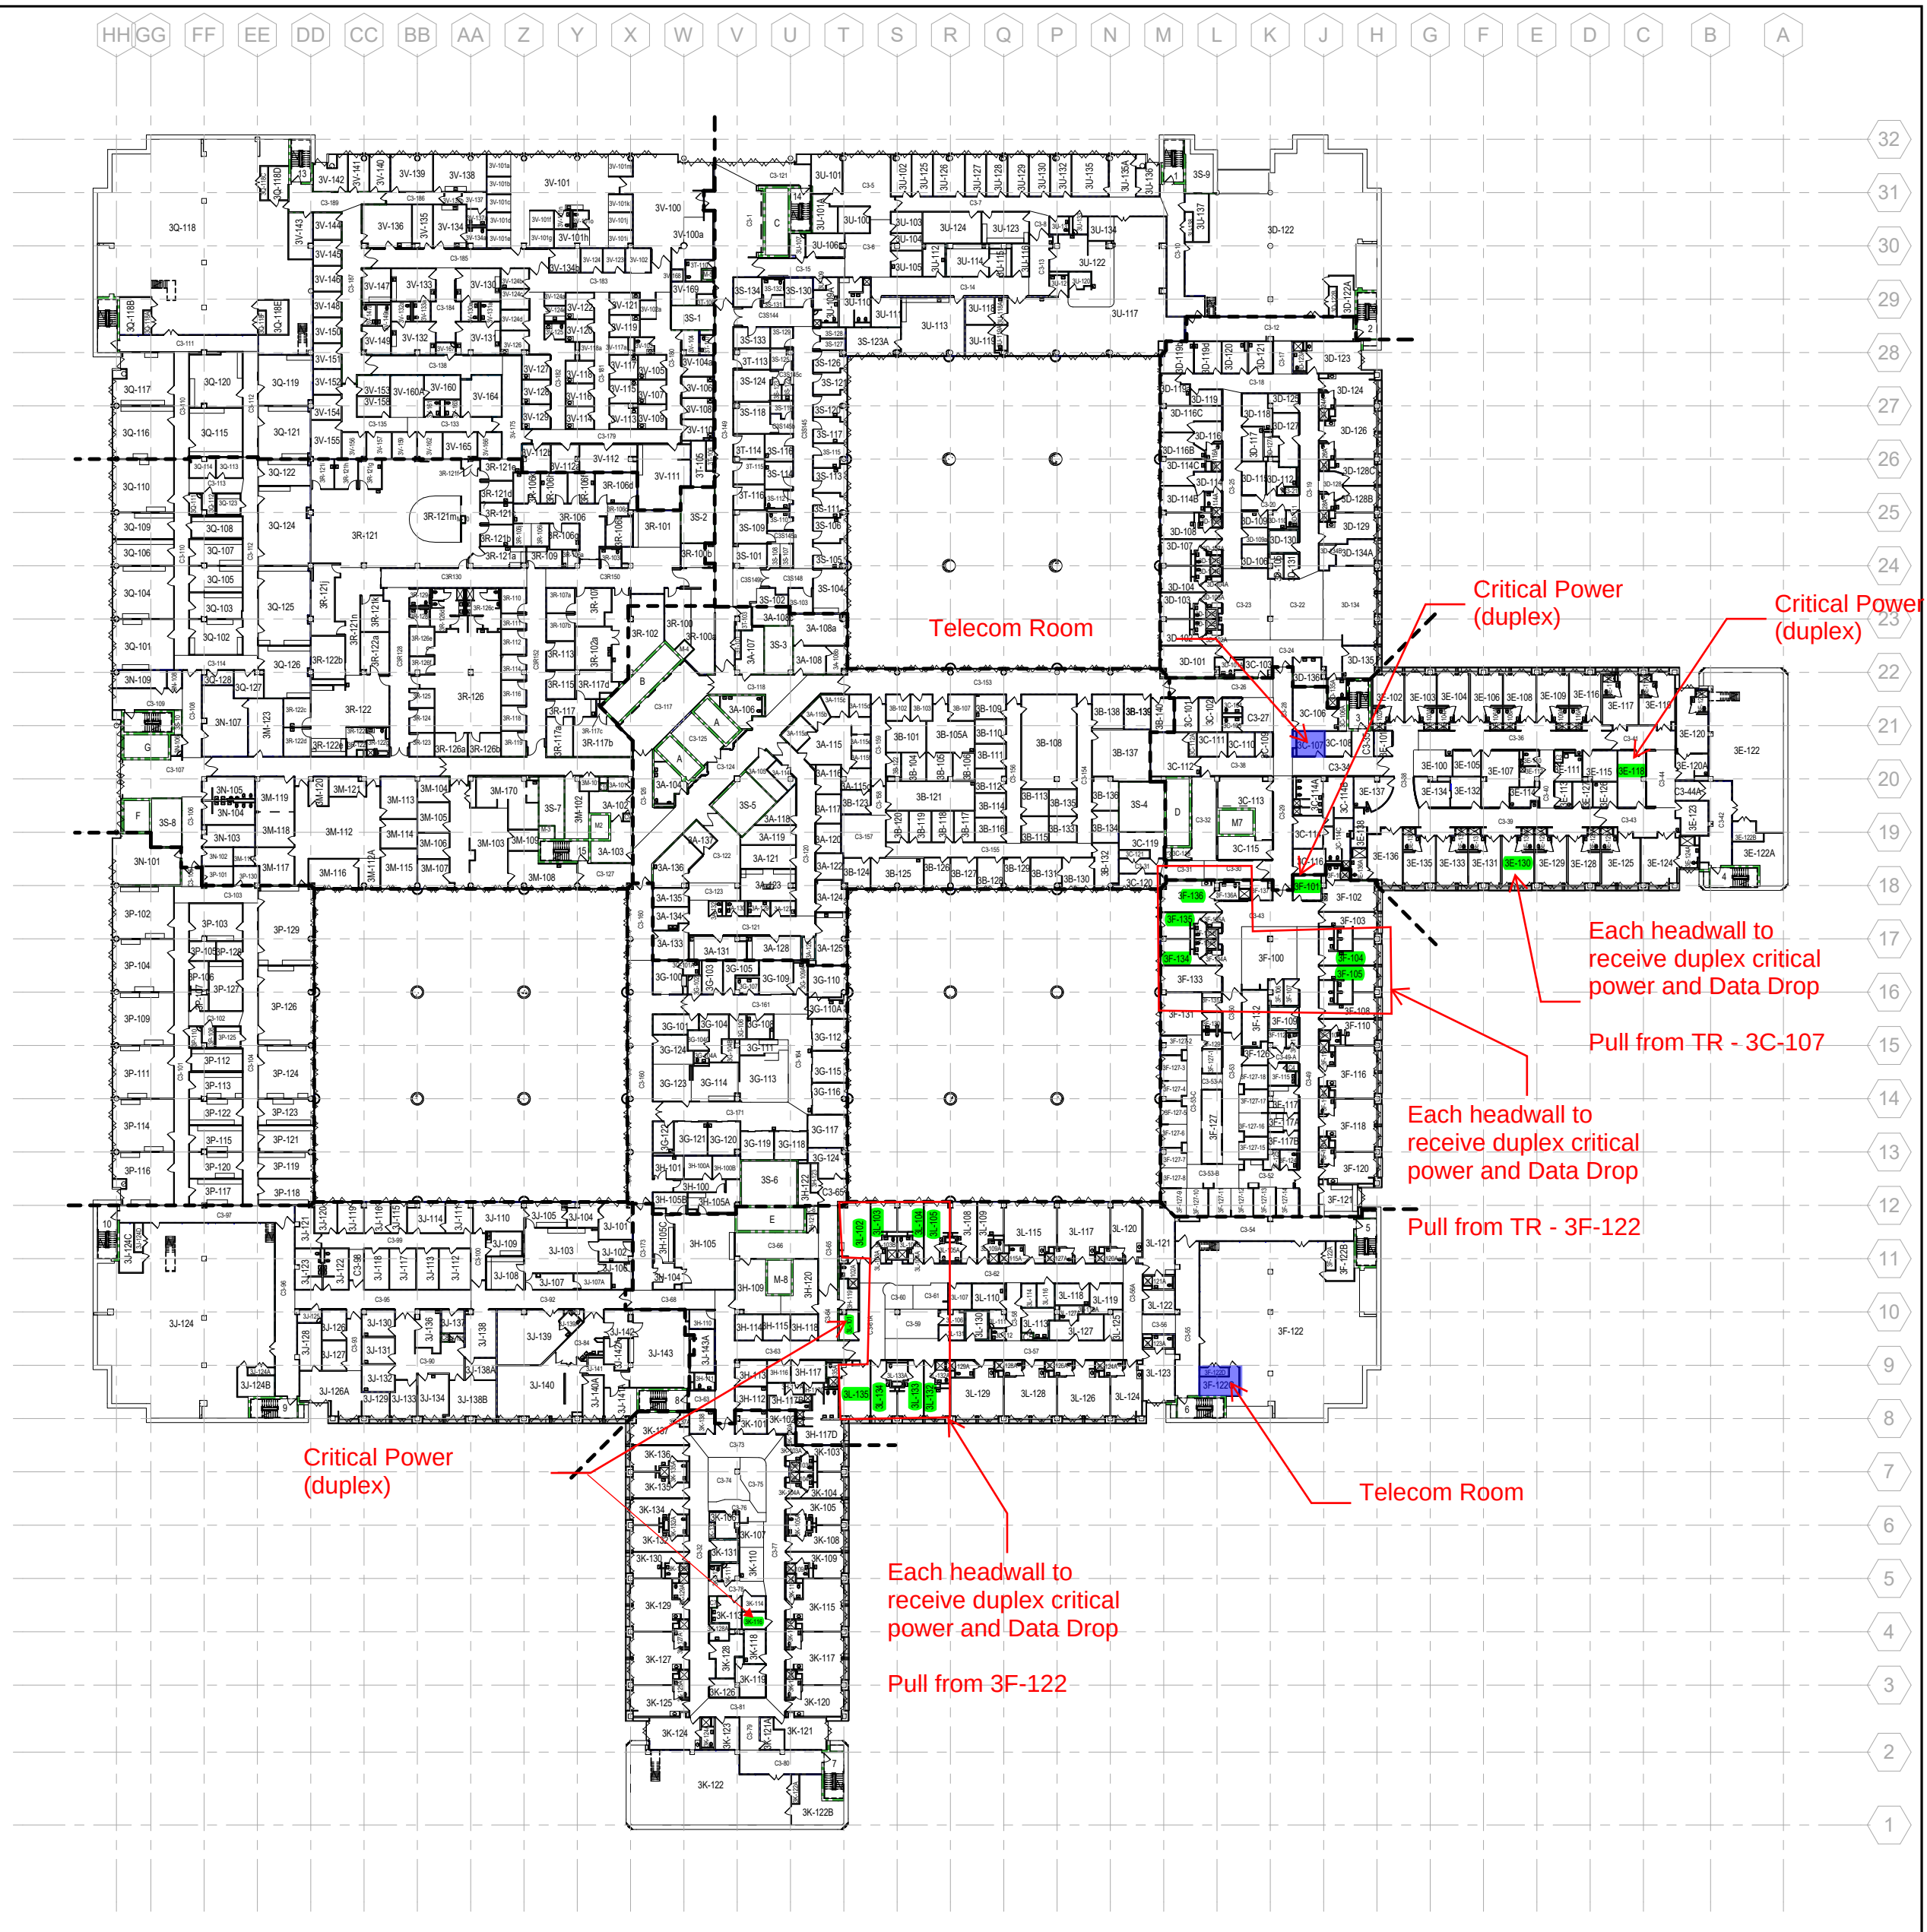
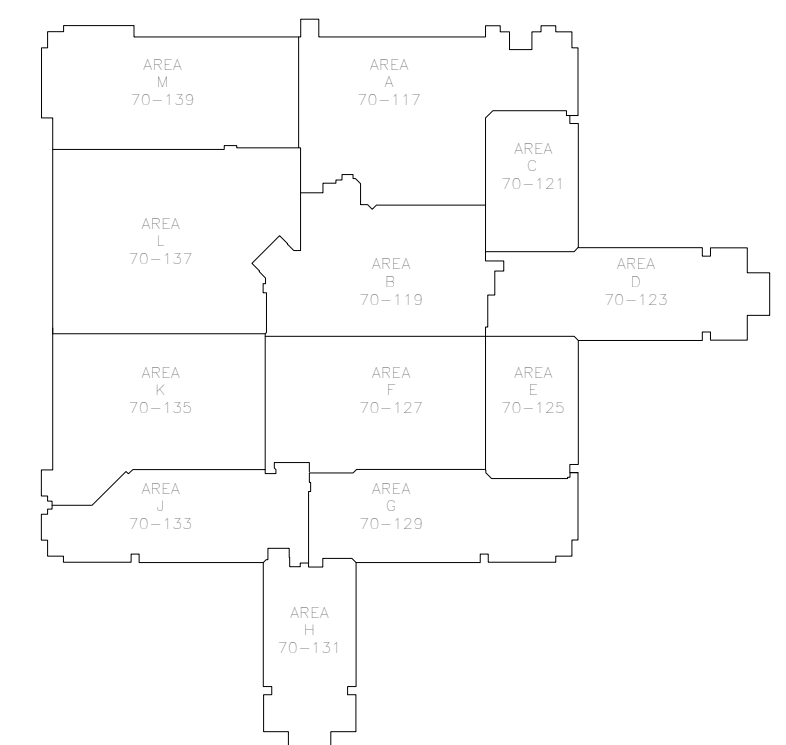


LEVEL 3
1/32" = 1'-0"

GENERAL NOTES: GENERAL CONTRACTOR AND/OR ALL SUBCONTRACTORS SHALL FIELD VERIFY ALL DIMENSIONS SHOWN ON THESE PLANS AND SHALL BE RESPONSIBLE FOR VARIATIONS BETWEEN PLAN DIMENSIONS AND ACTUAL FIELD DIMENSIONS. WHERE VARIATIONS ARE FOUND TO OCCUR, THE CONTRACTOR SHALL NOTIFY THE PROJECT ENGINEER IN WRITING PRIOR TO PROCEEDING WITH CONSTRUCTION. NO ADJUSTMENT TO THE WORK WILL BE MADE WITHOUT THE PRIOR APPROVAL OF THE PROJECT ENGINEER. GENERAL CONTRACTOR SHALL BE RESPONSIBLE FOR GENERAL DEMOLITION INCLUDING REMOVAL OF WALLS, PARTITIONS, DOORS & CEILING & FLOORS. ANY AND ALL CUTTING OF CONCRETE FLOORS, WALLS OR STRUCTURE SHALL BE THE GENERAL CONTRACTOR'S RESPONSIBILITY. CORE DRILLING THROUGH CONCRETE WALLS, FLOORS OR STRUCTURE FOR PIPING OR CONDUIT SHALL BE THE RESPONSIBILITY OF THE SUBCONTRACTOR BY TRADE. PRESTOPPING OF THESE OPENINGS SHALL BE DONE BY THE RESPECTIVE SUBCONTRACTOR. REMOVAL OF DEBRIS RESULTING FROM DEMOLITION, CUTTING, AND/OR DRILLING IS THE RESPONSIBILITY OF THE GENERAL CONTRACTOR. PATCHING AND REPAIR OF CONCRETE WALLS, FLOOR, OR STRUCTURE SHALL BE THE RESPONSIBILITY OF THE GENERAL CONTRACTOR. THIS WILL BE ACCOMPLISHED UPON COMPLETION OF THE INSTALLATION OF ANY AND ALL UTILITIES INSTALLED BY THE VARIOUS SUBCONTRACTORS.	 PERFORMANCE DRIVEN DESIGN. LHBcorp.com	 TRUE NORTH PLAN NORTH	I HEREBY CERTIFY THAT THIS PLAN, SPECIFICATION, OR ANY OTHER DOCUMENT PREPARED BY ME OR UNDER MY SUPERVISION AND THAT I AM A DULY LICENSED PROFESSIONAL ENGINEER UNDER THE LAWS OF THE STATE OF MINNESOTA. REGISTRATION NUMBER: _____ Drawing Scale: 1/32" = 1'-0" Plot Scale: _____ Drawing Title: 3rd Floor Composite Plan Approved: Division Chief _____ Approved: Service Director _____	Project Title: MVA MODEL Location: 1 Veterans Dr Minneapolis, MN 55417 Date: 04/13/2020 Checked: NA Drawn: MJH	Project No.: 618-00-000 Building Number: 70 DRAWING NO.: 0000 - 003	Project Status 04/13/2020 Office of Facilities Management Department of Veterans Affairs
	REVISIONS DATE					

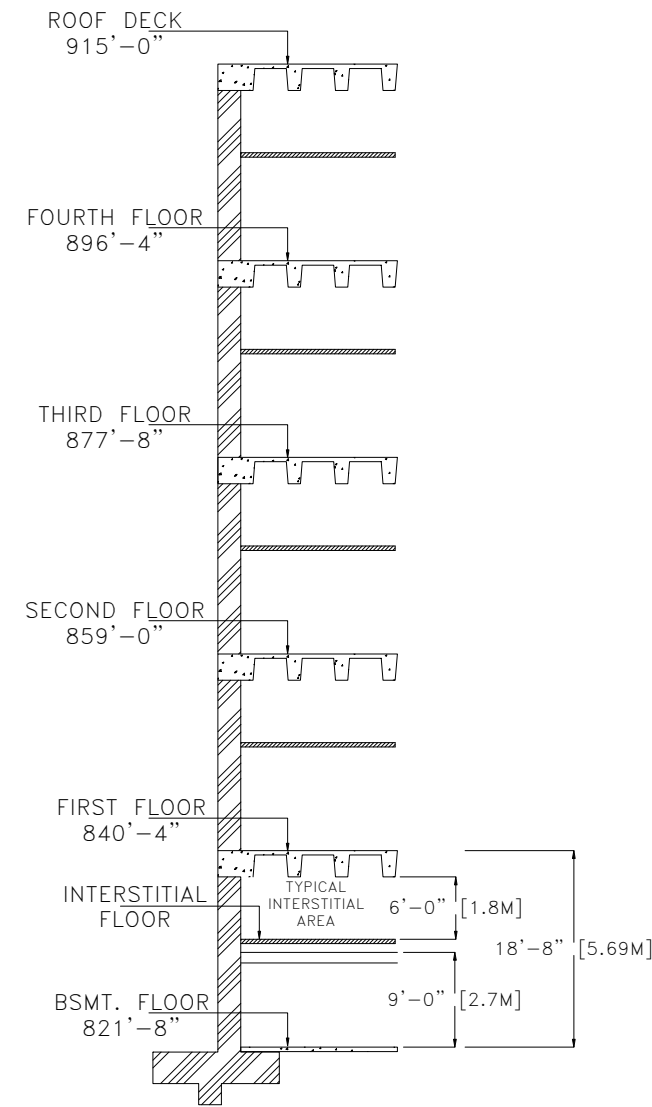

TYPICAL ELEVATION
NOT TO SCALE

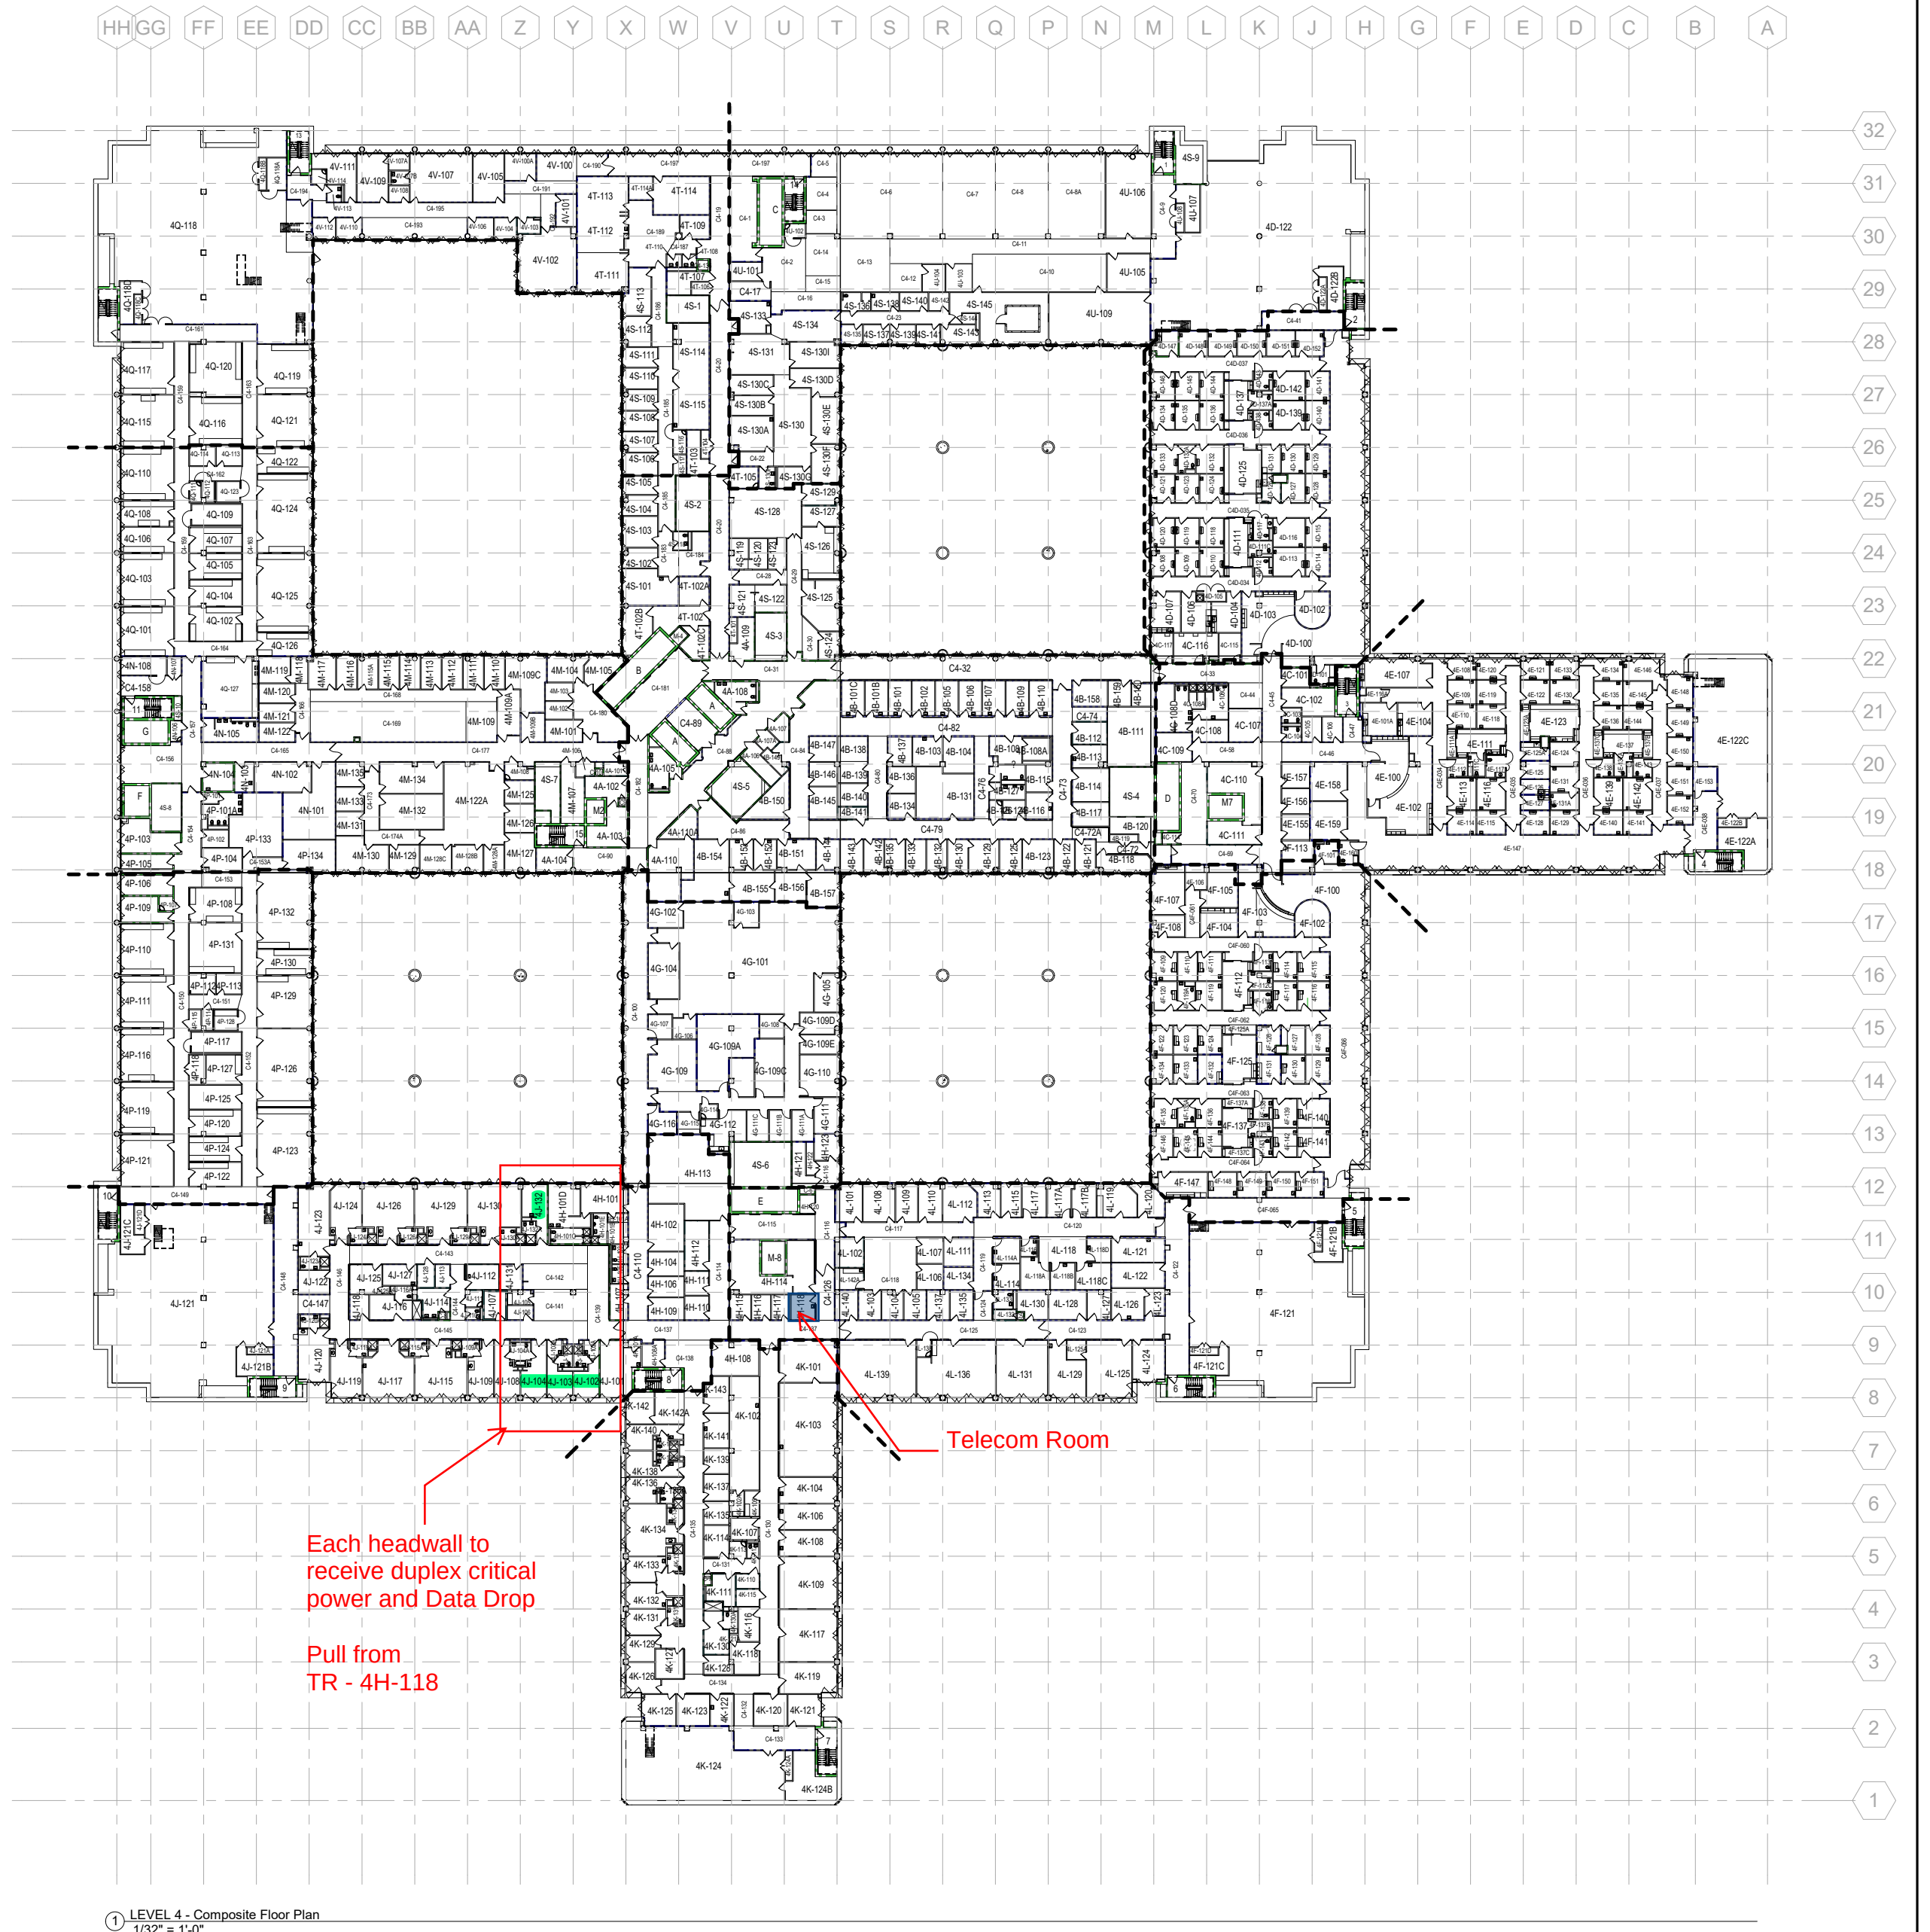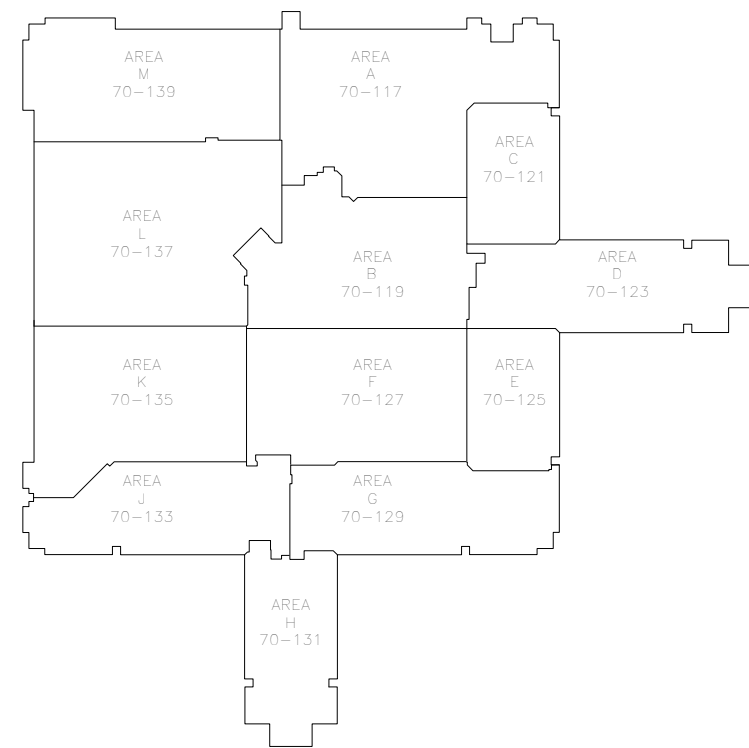


1 LEVEL 4 - Composite Floor Plan
1/32" = 1'-0"

REVISIONS	DATE

GENERAL NOTES:

GENERAL CONTRACTOR AND/OR ALL SUBCONTRACTORS SHALL FIELD VERIFY ALL DIMENSIONS SHOWN ON THESE PLANS AND SHALL BE RESPONSIBLE FOR VARIATIONS BETWEEN PLAN DIMENSIONS AND ACTUAL FIELD DIMENSIONS. WHERE VARIATIONS ARE FOUND TO OCCUR, THE CONTRACTOR SHALL NOTIFY THE PROJECT ENGINEER IN WRITING PRIOR TO PROCEEDING WITH CONSTRUCTION. NO ADJUSTMENT TO THE WORK WILL BE MADE WITHOUT THE PRIOR APPROVAL OF THE PROJECT ENGINEER.

GENERAL CONTRACTOR SHALL BE RESPONSIBLE FOR GENERAL DEMOLITION INCLUDING REMOVAL OF WALLS, PARTITIONS, DOORS & CEILING & FLOORS. ANY AND ALL CUTTING OF CONCRETE FLOORS, WALLS OR STRUCTURE SHALL BE THE GENERAL CONTRACTORS RESPONSIBILITY. CORE DRILLING THROUGH CONCRETE FLOORS, WALLS OR STRUCTURE FOR PIPING OR CONDUIT SHALL BE THE RESPONSIBILITY OF THE SUBCONTRACTOR BY TRADE. PRESTOPPING OF THESE OPENINGS SHALL BE DONE BY THE RESPECTIVE SUBCONTRACTOR. REMOVAL OF DEBRIS RESULTING FROM DEMOLITION, CUTTING, AND/OR DRILLING IS THE RESPONSIBILITY OF THE GENERAL CONTRACTOR. PATCHING AND REPAIR OF CONCRETE WALLS, FLOOR, OR STRUCTURE SHALL BE THE RESPONSIBILITY OF THE GENERAL CONTRACTOR. THIS WILL BE ACCOMPLISHED UPON COMPLETION OF THE INSTALLATION OF ANY AND ALL UTILITIES INSTALLED BY THE VARIOUS SUBCONTRACTORS.

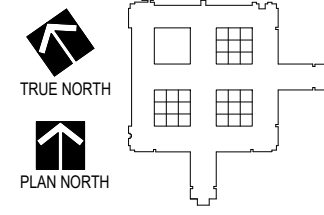

I HEREBY CERTIFY THAT THIS PLAN, SPECIFICATION, OR OTHER DOCUMENT IS A TRUE AND CORRECT REPRESENTATION OF THE DESIGN AND CONSTRUCTION OF THE PROJECT AND THAT I AM A DULY REGISTERED ARCHITECT UNDER THE LAWS OF THE STATE OF MINNESOTA.

REGISTRATION NUMBER:

Drawing Scale
1/32" = 1'-0"

Plot Scale

Drawing Title
4th Floor Composite Floor Plan

Approved: Division Chief

Approved: Service Director

Project Title
Minneapolis Veterans Health Administration

Location
1 Veterans Dr., Minneapolis, MN 55033

Date
04/13/2020

Checked
Checker

Drawn
MJH

Project No.
Project Number

Building Number
70

DRAWING NO.
0000 - 004

Project Status 04/13/2020

Office of Facilities Management

Department of Veterans Affairs

HH GG FF EE DD CC BB AA Z Y X W V U T S R Q P N M L K J H G F E D C B A

32
31
30
29
28
27
26
25
24
23
22
21
20
19
18
17
16
15
14
13
12
11
10
9
8
7
6
5
4
3
2
1

PENTHOUSE ROOF
937'-8"

ROOF DECK
915'-0"

FOURTH FLOOR
896'-4"

THIRD FLOOR
877'-8"

SECOND FLOOR
859'-0"

FIRST FLOOR
840'-4"

INTERSTITIAL FLOOR
TYPICAL INTERSTITIAL AREA
6'-0" [1.8M]
18'-8" [5.69M]

BSMT. FLOOR
821'-8"

9'-0" [2.7M]

TYPICAL ELEVATION
NOT TO SCALE

Area A
70-215

Area L
70-216

Area B
70-216

Area F
70-217

REVISIONS

DATE

GENERAL NOTES:

GENERAL CONTRACTOR AND/OR ALL SUBCONTRACTORS SHALL FIELD VERIFY ALL DIMENSIONS SHOWN ON THESE PLANS AND SHALL BE RESPONSIBLE FOR VARIATIONS BETWEEN PLAN DIMENSIONS AND ACTUAL FIELD DIMENSIONS. WHERE VARIATIONS ARE FOUND TO OCCUR, THE CONTRACTOR SHALL NOTIFY THE PROJECT ENGINEER IN WRITING PRIOR TO PROCEEDING WITH CONSTRUCTION. NO ADJUSTMENT TO THE WORK WILL BE MADE WITHOUT THE PRIOR APPROVAL OF THE PROJECT ENGINEER.

GENERAL CONTRACTOR SHALL BE RESPONSIBLE FOR GENERAL DEMOLITION INCLUDING REMOVAL OF WALLS, PARTITIONS, DOORS & CEILING & FLOORS. ANY AND ALL CUTTING OF CONCRETE FLOORS, WALLS OR STRUCTURE SHALL BE THE GENERAL CONTRACTOR'S RESPONSIBILITY. CORE DRILLING THROUGH CONCRETE WALLS, FLOORS OR STRUCTURE FOR PIPING OR CONDUIT SHALL BE THE RESPONSIBILITY OF THE SUBCONTRACTOR BY TRADE. PRESTOPPING OF THESE OPENINGS SHALL BE DONE BY THE RESPECTIVE SUBCONTRACTOR. REMOVAL OF DEBRIS RESULTING FROM DEMOLITION, CUTTING, AND/OR DRILLING IS THE RESPONSIBILITY OF THE GENERAL CONTRACTOR. PATCHING AND REPAIR OF CONCRETE WALLS, FLOOR, OR STRUCTURE SHALL BE THE RESPONSIBILITY OF THE GENERAL CONTRACTOR. THIS WILL BE ACCOMPLISHED UPON COMPLETION OF THE INSTALLATION OF ANY AND ALL UTILITIES INSTALLED BY THE VARIOUS SUBCONTRACTORS.

TRUE NORTH

PLAN NORTH

I HEREBY CERTIFY THAT THIS PLAN, SPECIFICATION, OR REPORT WAS PREPARED BY ME OR UNDER MY DIRECT SUPERVISION AND THAT I AM A DULY REGISTERED ARCHITECT UNDER THE LAWS OF THE STATE OF MINNESOTA.

REGISTRATION NUMBER:

Drawing Scale
1/32" = 1'-0"

Plot Scale

Drawing Title
Penthouse

Approved: Division Chief

Approved: Service Director

Project Title
Minneapolis Veterans Health Administration

Location

Date
4/13/2020

Checked
Checker

Drawn
MJH

Project No.
000

Building Number
70

DRAWING NO.
000-005

Office of
Facilities
Management

Department of
Veterans Affairs

4/13/2020



BLDG. 49

Telecom Room



Department of
Veterans Affairs