


N
P

Detail Plans for Daugherty WRE WETLAND RESTORATION PROJECT


This project involves excavation of a pools, tile exploration, and habitat mounds.

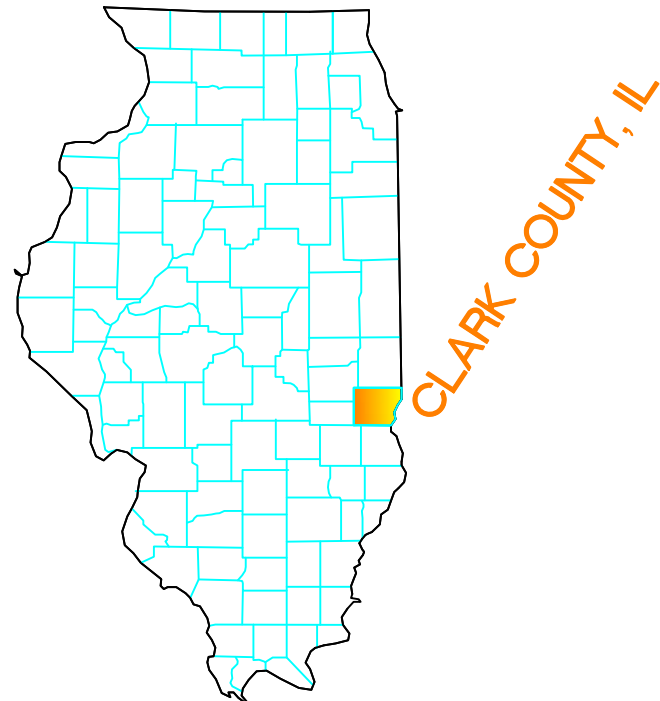

Location Map

Contractor responsible for
contacting Illinois JULIE
811-1-800-892-0123
www.illinois1call.com

Contractor must provide NRCS
with DIG number(s) prior to start
of construction.

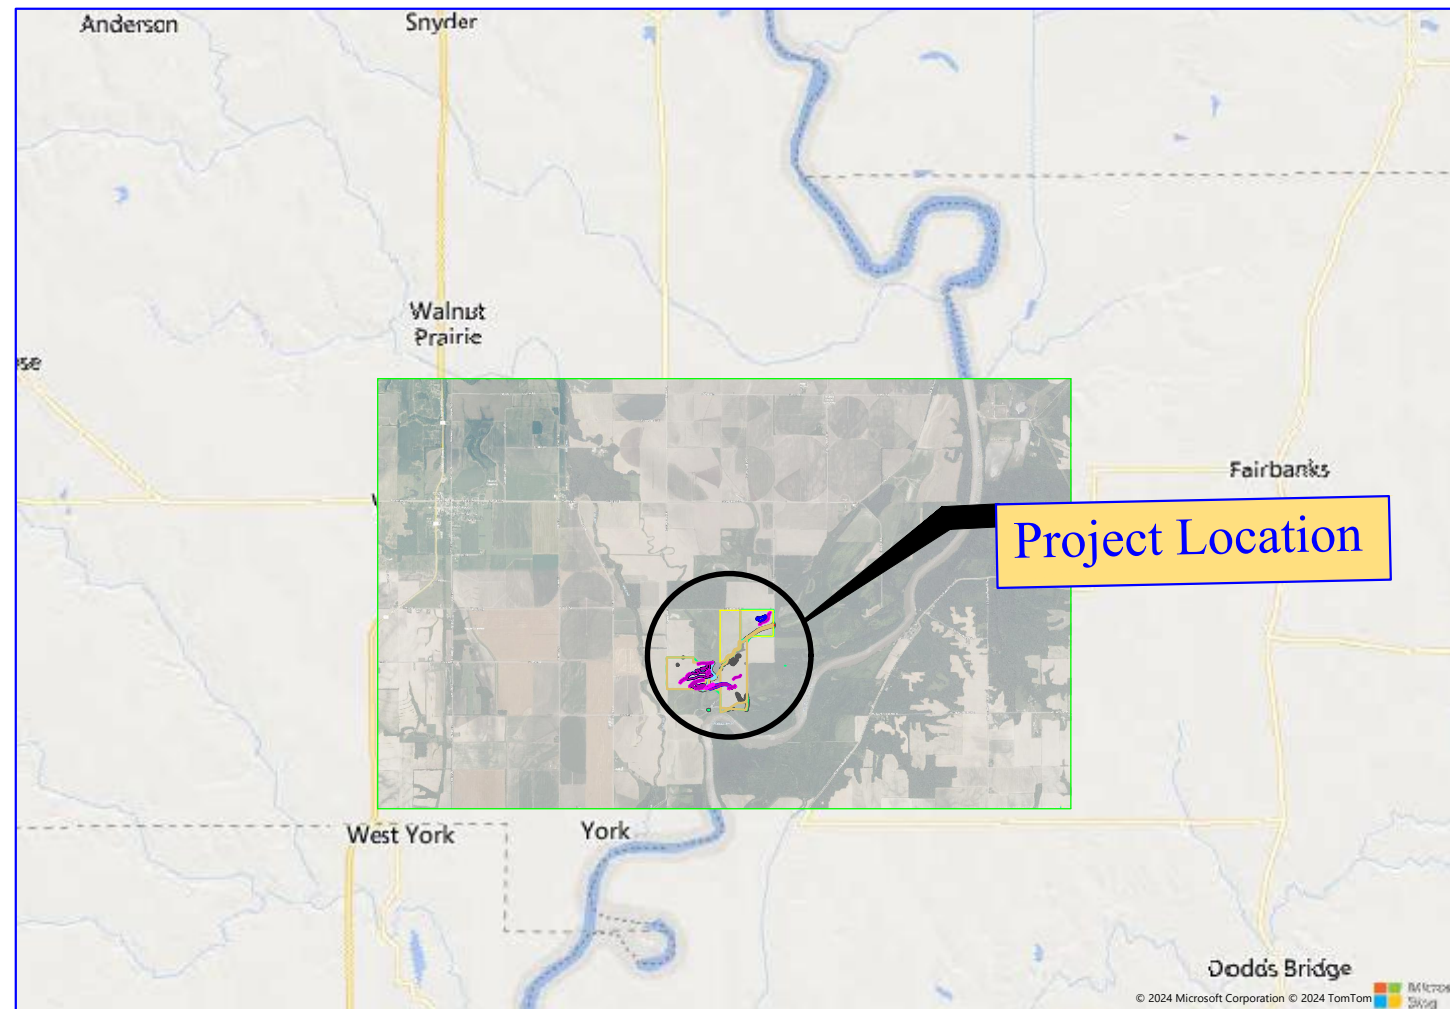

CLARK COUNTY, ILLINOIS
T9N, R11W, Section 27


Index of Sheets

- | | |
|-------|--------------------------------|
| 1 | Title Sheet |
| 2 | Location Map |
| 3 | Site Layout |
| 4-6 | Plan View 1-3 |
| 7-9 | Pool AA profile and X-Sections |
| 10-13 | HM1 Profile and X-Sections |
| 14-17 | HM3 Profile and X-Sections |
| 18-19 | HM3A Profile and X-Sections |
| 20-22 | HM4 Profile and X-Sections |
| 23-26 | HM5 Profile and X-Sections |
| 27-28 | HM6 Profile and X-Sections |
| 29-30 | HM7 Profile and X-Sections |
| 31-32 | HM8 Profile and X-Sections |
| 33-34 | HM9A Profile and X-Sections |
| 35-37 | Pool B1 Profile and X-Sections |
| 38-41 | Pool B2 Profile and X-Sections |
| 42-44 | Pool C Profile and X-Sections |
| 45-48 | Pool D Profile and X-Sections |

Designed	Kerry Bushue	Date	10/23/23
Drawn	Kerry Bushue	Date	10/23/23
Checked	M. Daanbroek	Date	8/20/25
Approved	M. Daanbroek	Date	8/20/25

TITLE SHEET
Daugherty Wetland


York Township, Clark County, IL
T9N, R11W, Section 27

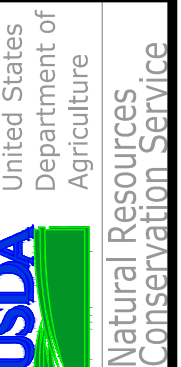


File No.

Drawing No.


Sheet ### of .

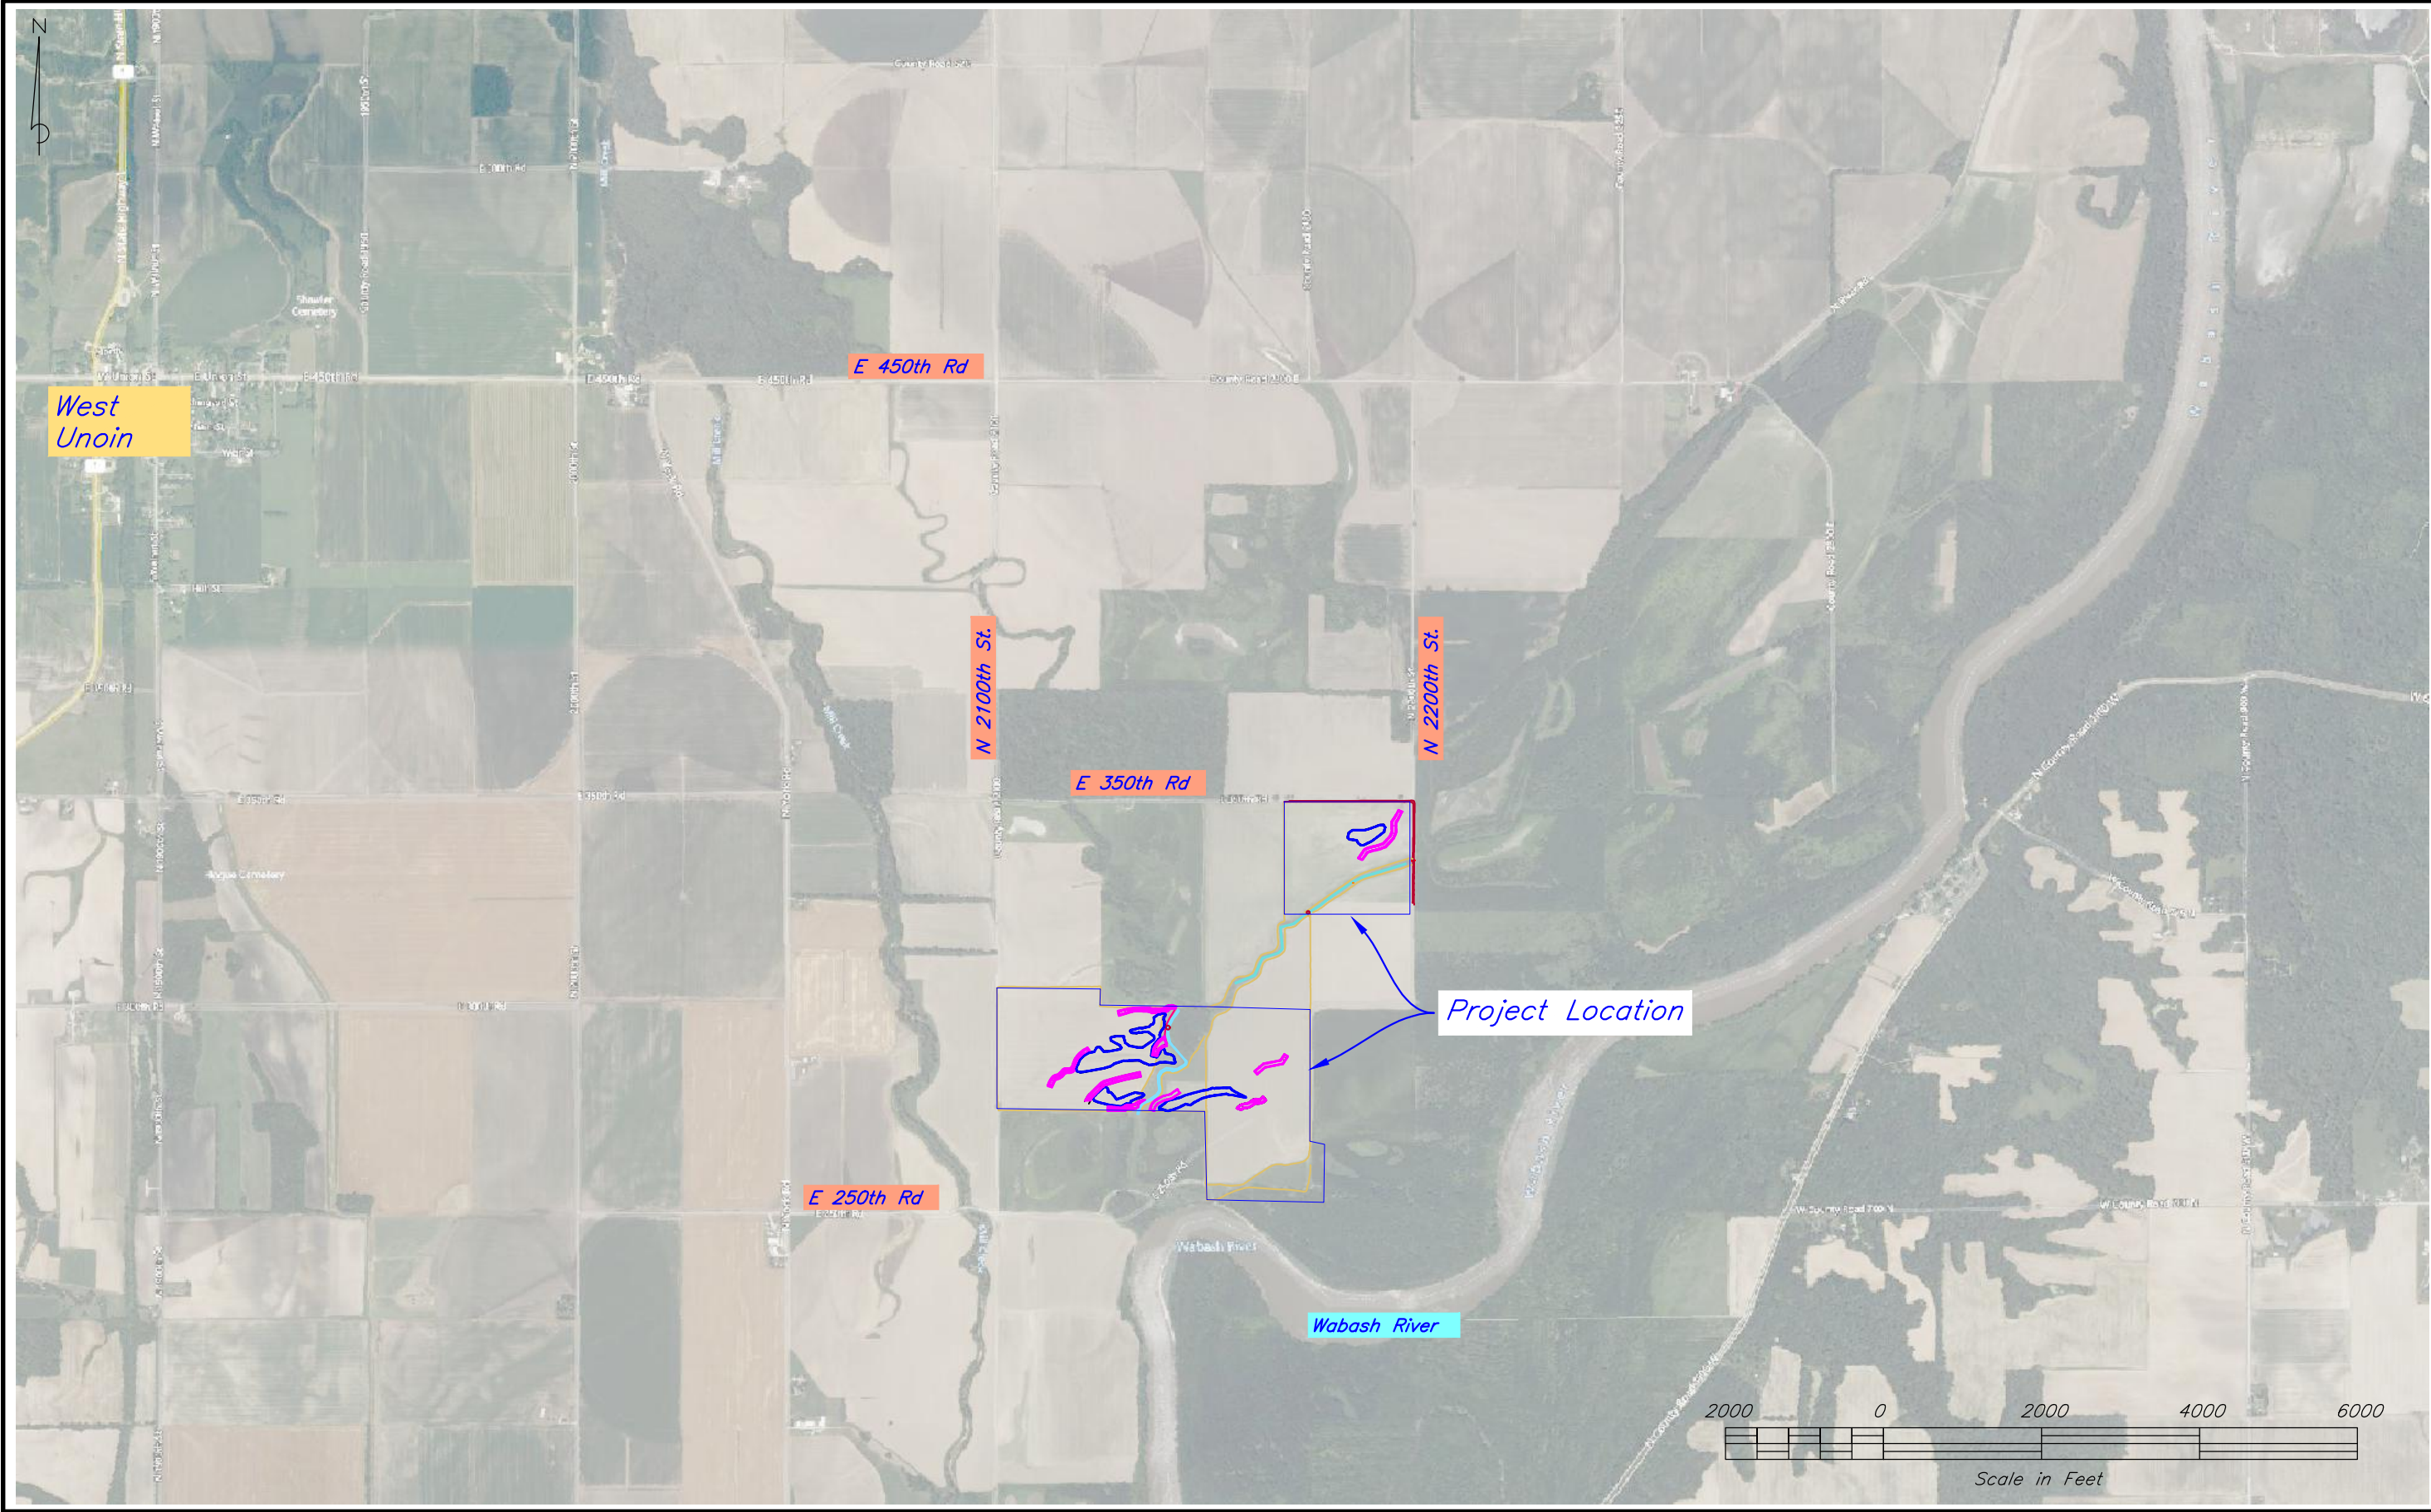


United States Department of Agriculture USDA Natural Resources Conservation Service		LOCATION MAP Daugherty Wetland		Designed <i>Kerry Bushue</i> 10/23/23	Date
File No.		Drawing No.		Drawn <i>Kerry Bushue</i> 10/23/23	
Sheet <i>1</i> of <i>1</i>		Checked <i>M. Dassenbrock</i> 8/2025		Approved <i>M. Dassenbrock</i> 8/2025	

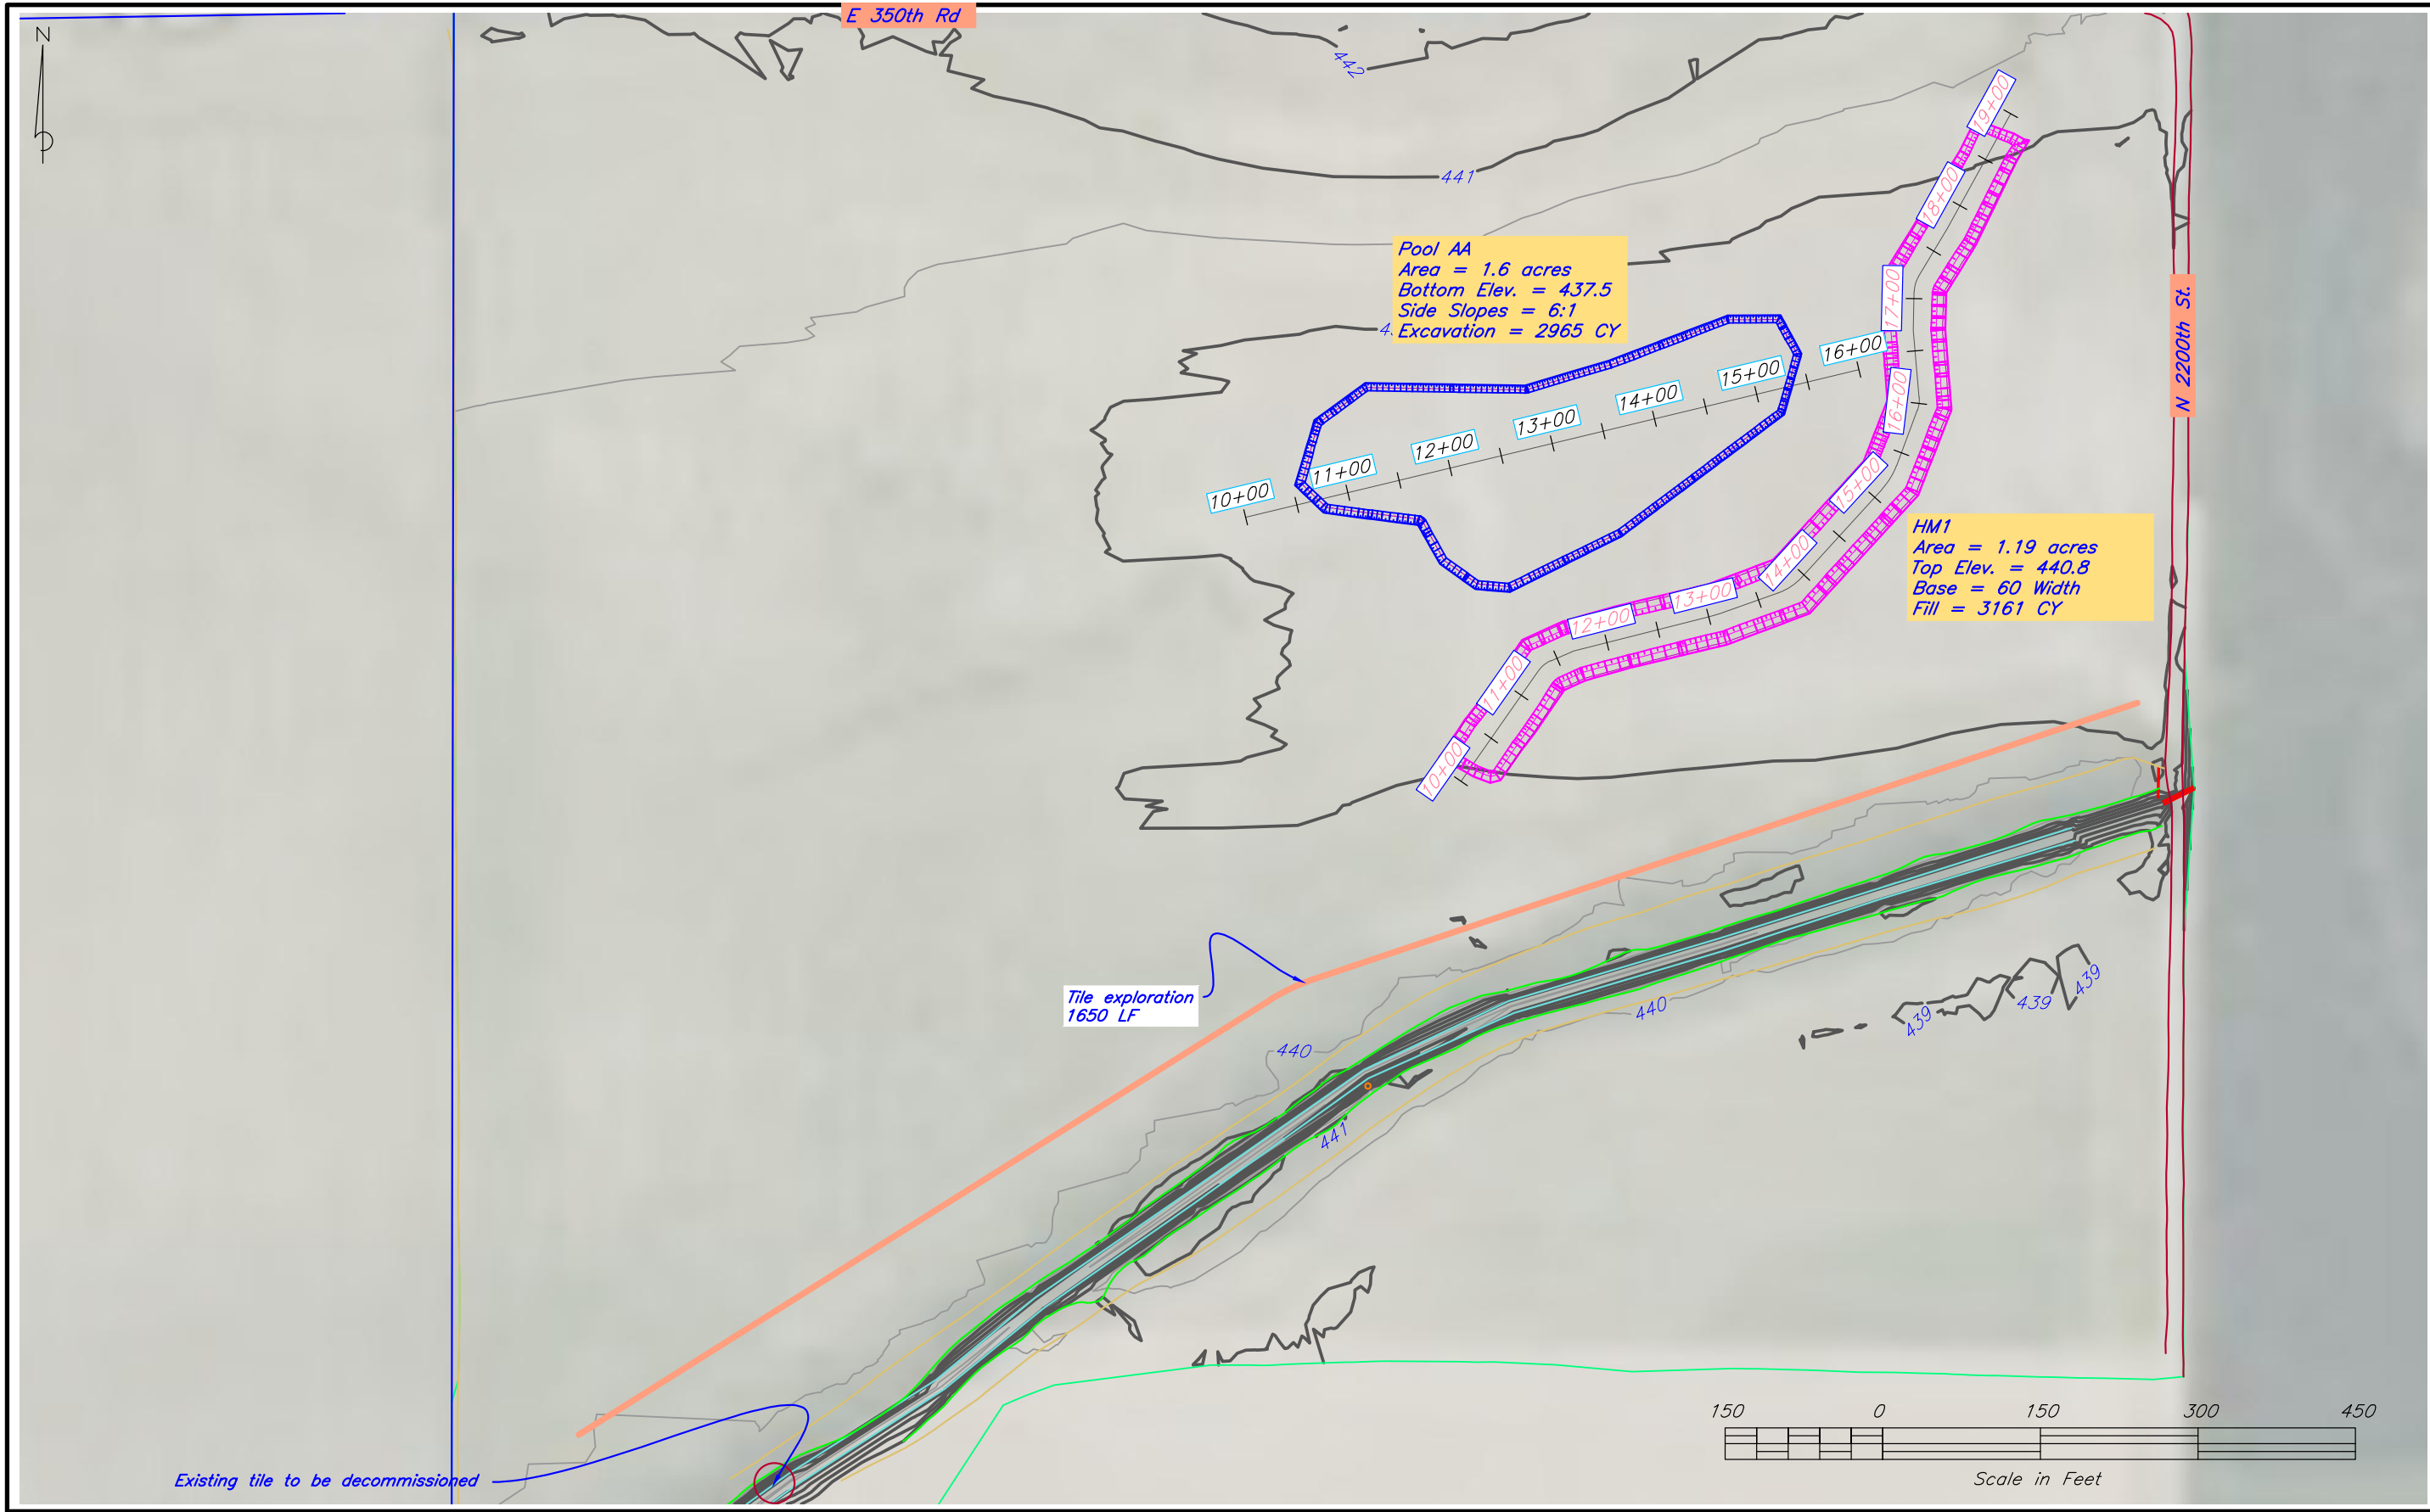


 United States Department of Agriculture Natural Resources Conservation Service	PLAN VIEW (1) Daugherty Wetland		Date 10/23/23
			Designed Kerry Bushue
			Drawn Kerry Bushue
			Checked M. Daanbroek 8/2025
		York Twnshp, . Sec.27 T 9N R 11W Clark County, IL.	Approved M. Daanbroek 8/2025
File No.		Drawing No.	
Sheet ### of		Date	

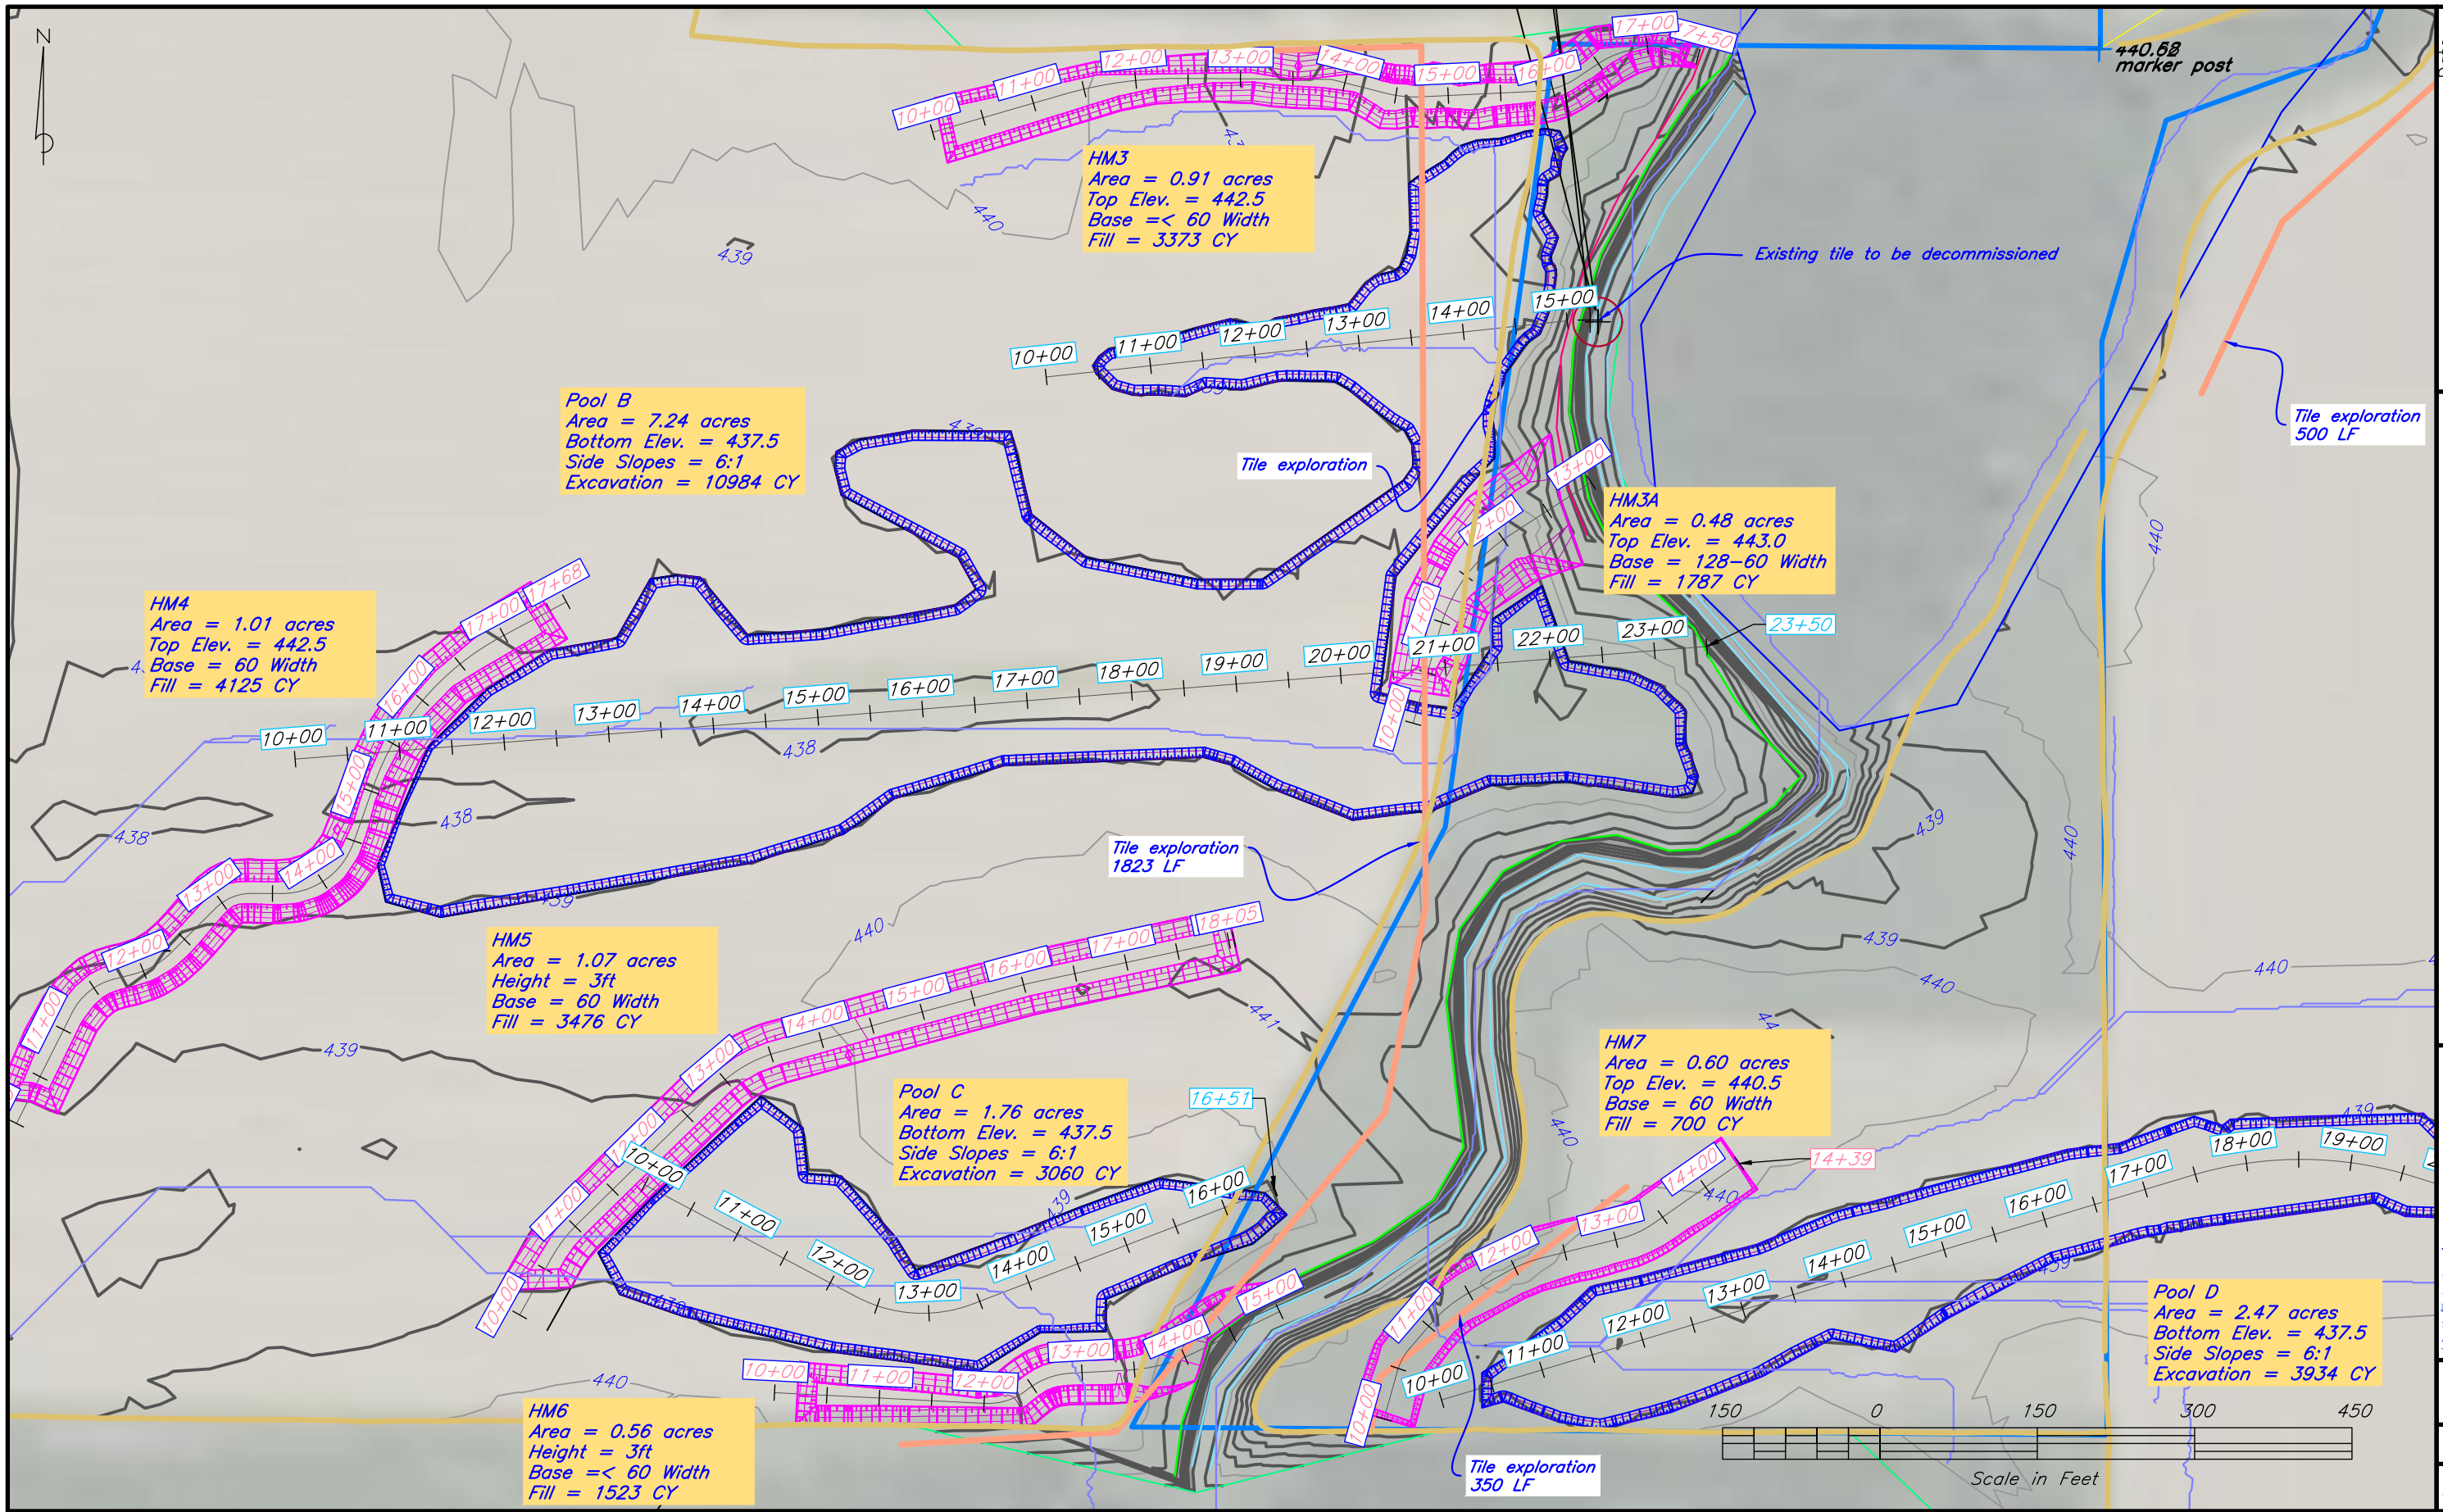

 United States Department of Agriculture Natural Resources Conservation Service	Date Designed Kerry Bushue 10/23/23 Drawn Kerry Bushue 10/23/23 Checked M. Daanbroek 8/20/25 Approved M. Daanbroek 8/20/25	
	PLAN VIEW (2) Daugherty Wetland	
	York Twnshp., Sec 27 T 9 N R 11 W Clark County, IL	
	File No. Drawing No. Sheet ### of .	

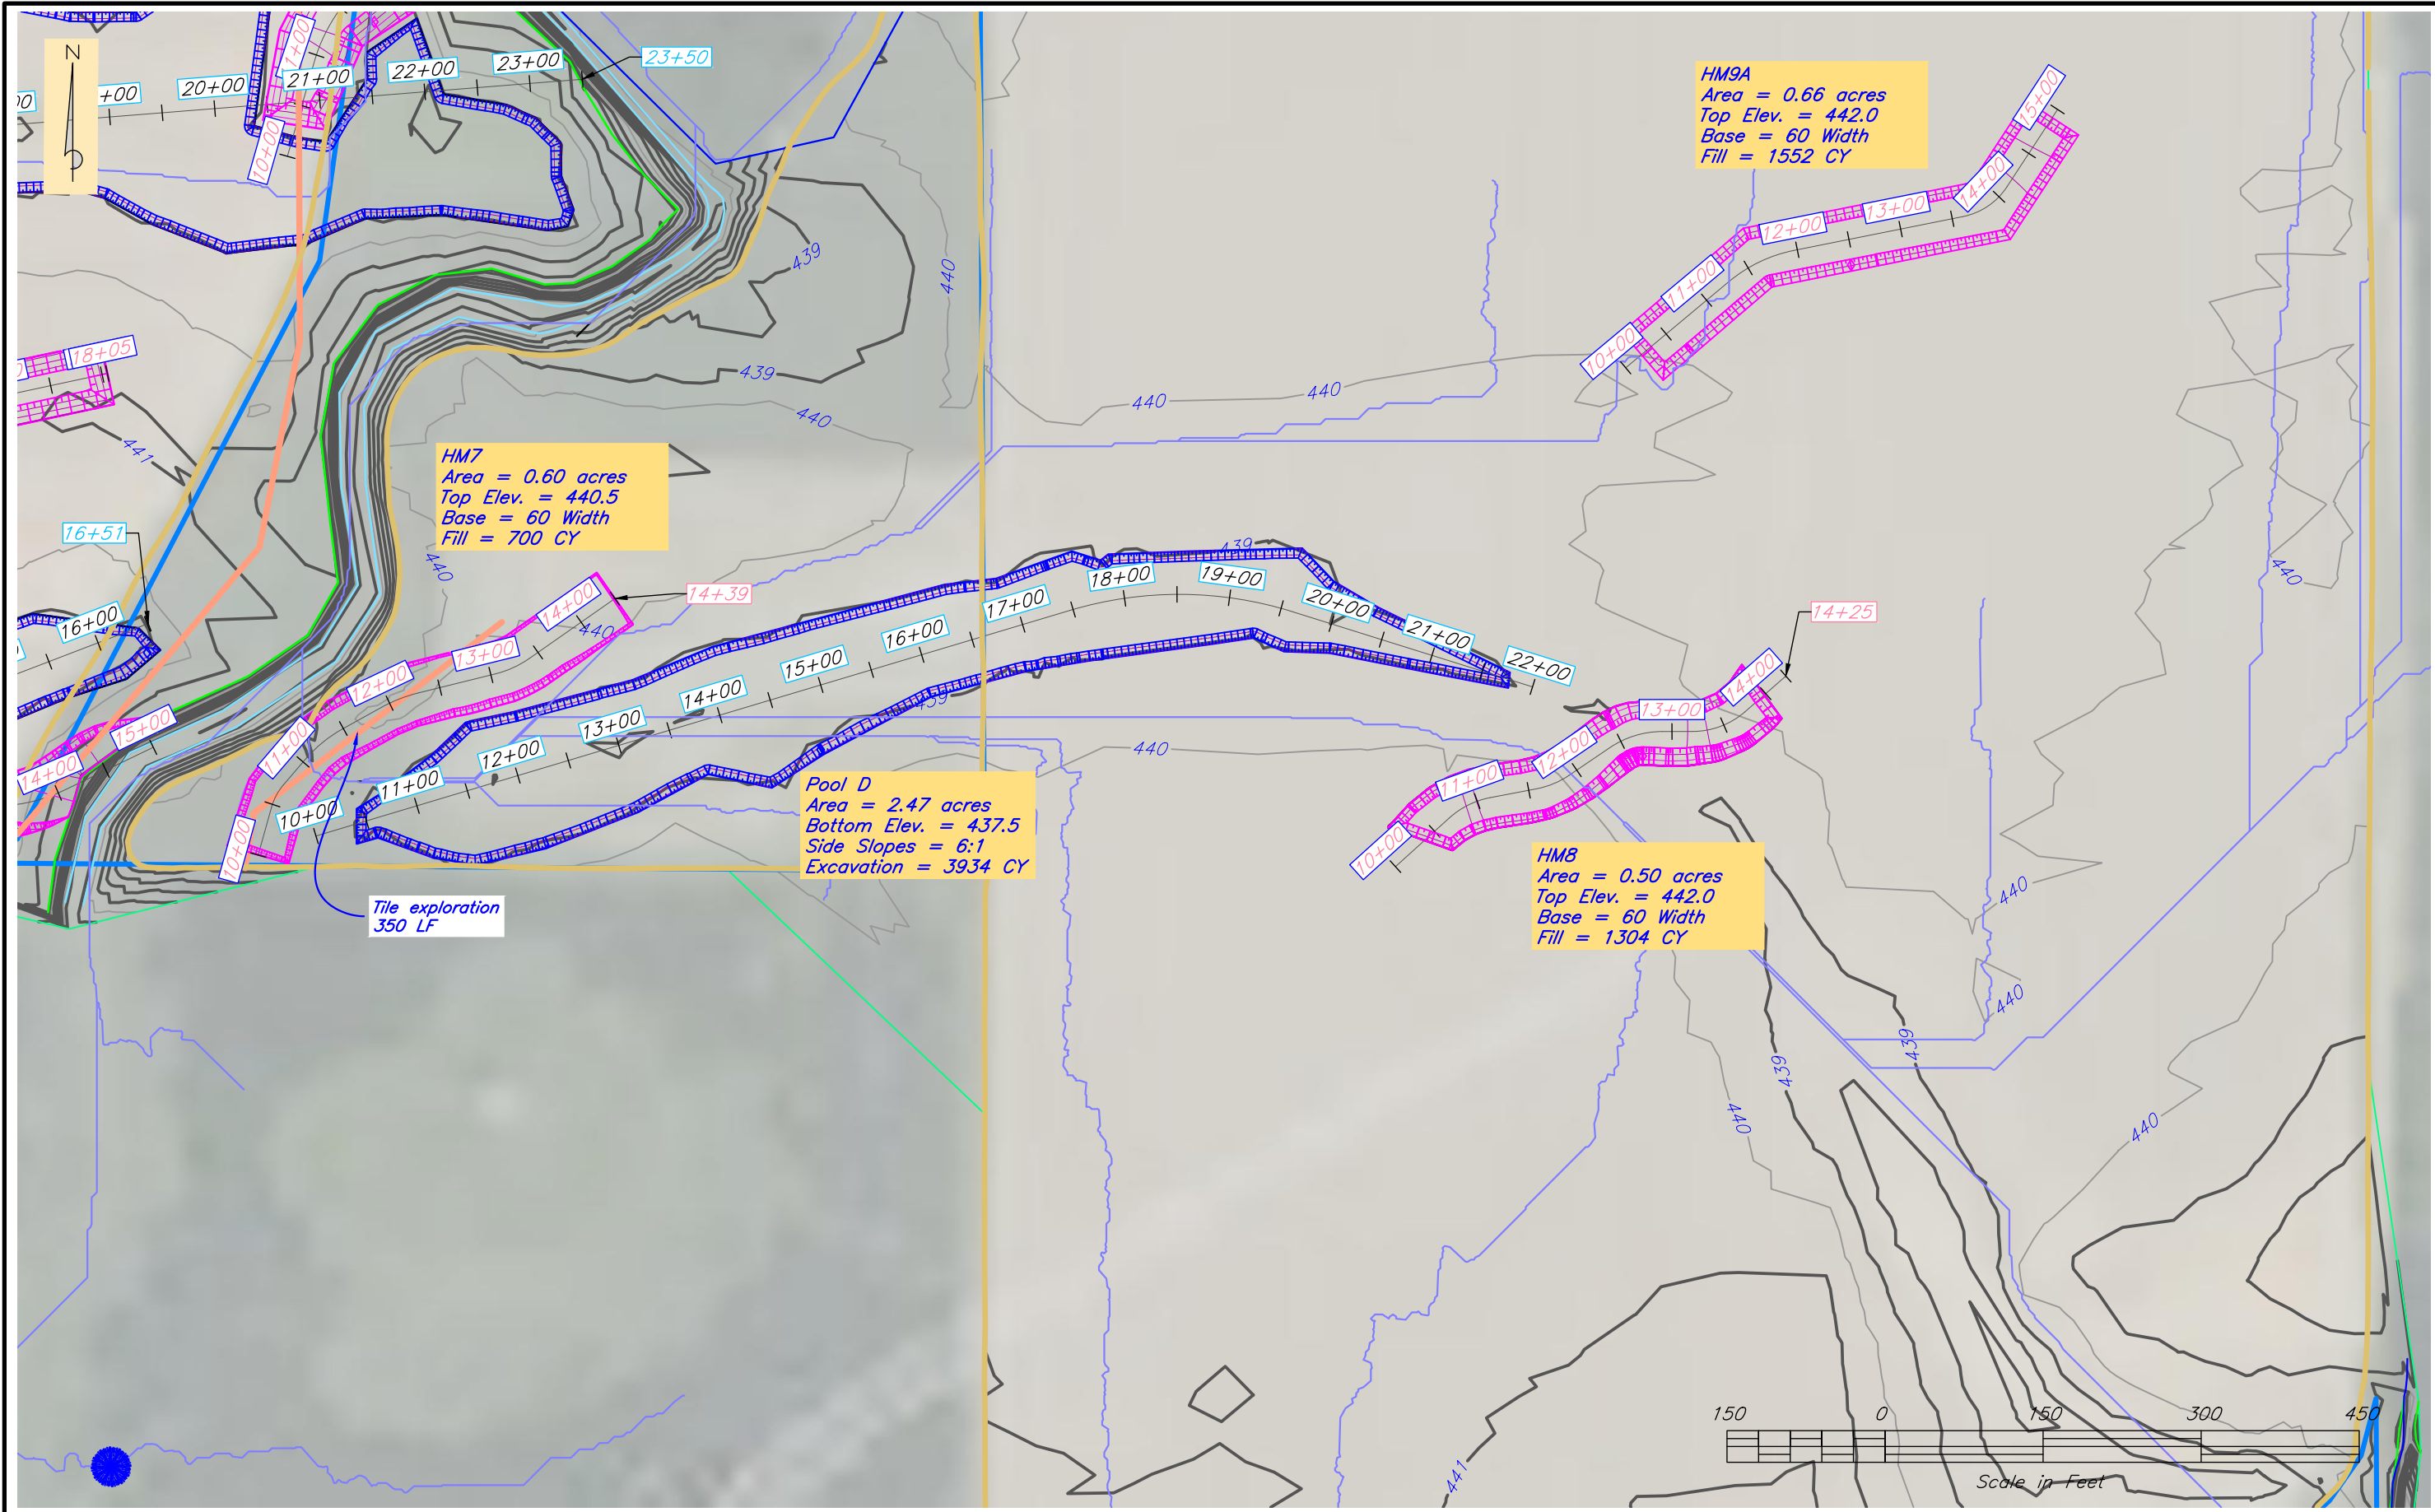

United States Department of Agriculture		Date Designed <u>Kerry Bushue</u> 10/23/23 Drawn <u>Kerry Bushue</u> 10/23/23 Checked <u>M. Dassenbrock</u> 8/2025	
Natural Resources Conservation Service		Approved <u>M. Dassenbrock</u> 8/2025	
File No.		York Twnshp, . Sec 27 T 9N R 11W Clark County, IL.	
Drawing No.		PLAN VIEW (3) Daugherty Wetland	
Sheet ### of .			

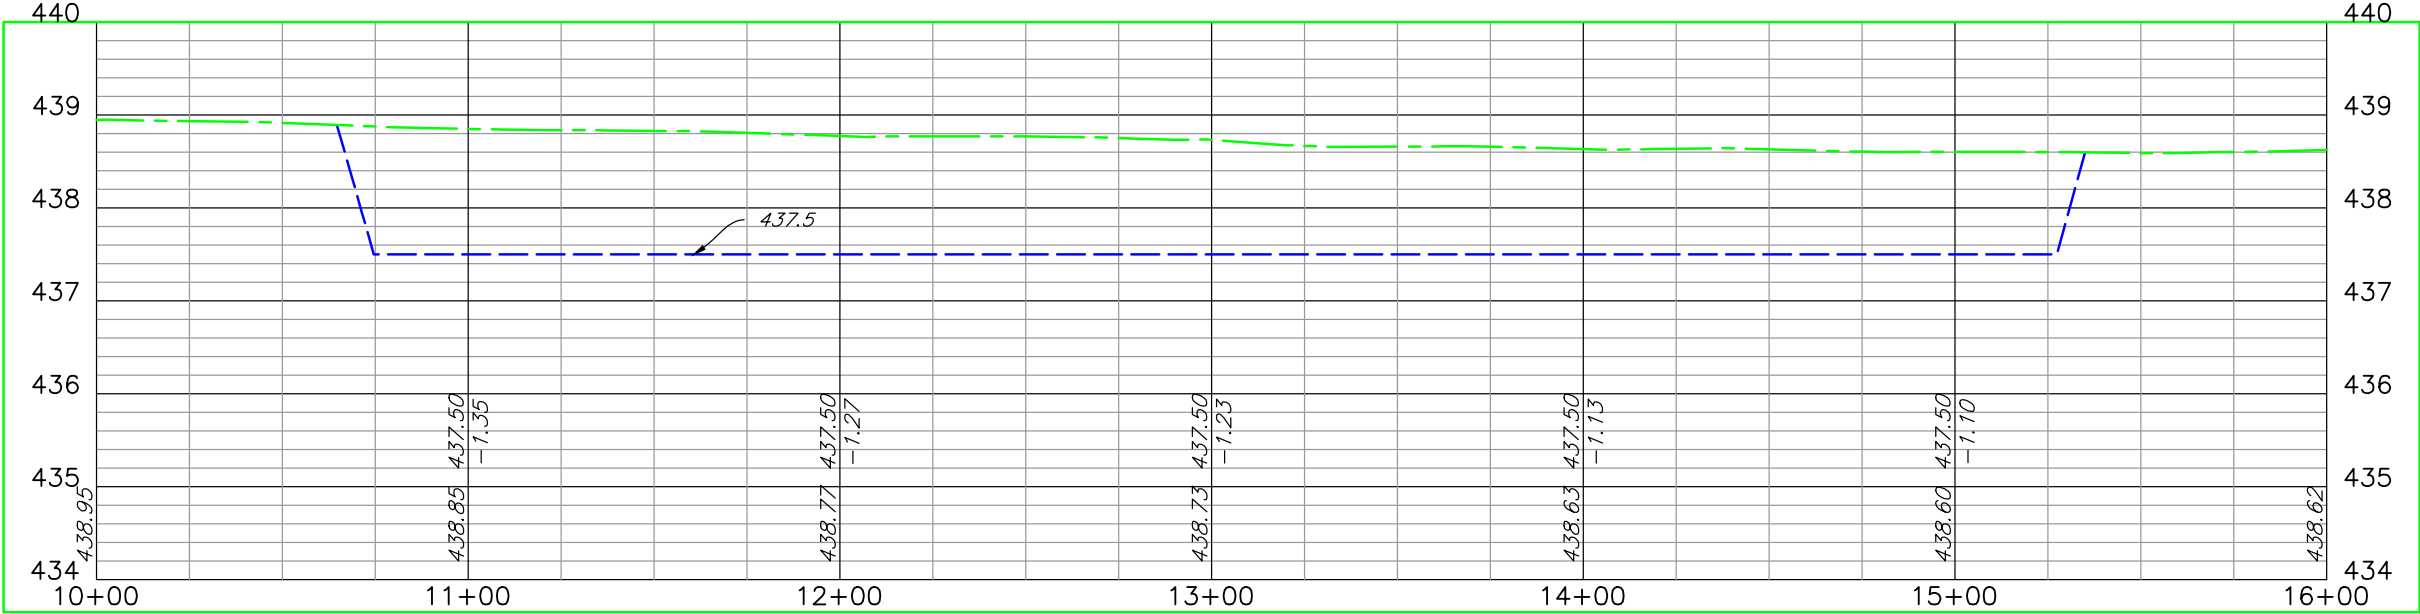

Existing Ground
Proposed Pool

POOL AA PROFILE
Daugherty Wetland



File No.

Drawing No.




Sheet ### of .

Designed Kerry Bushue 10/23/23
Drawn Kerry Bushue 10/23/23
Checked M.Daenbrook 8/20/25
Approved M.Daenbrook 8/20/25


York Twnshp., Sec 27 T 9 N R 11 W Clark County, IL.

Existing Ground



Proposed Pool

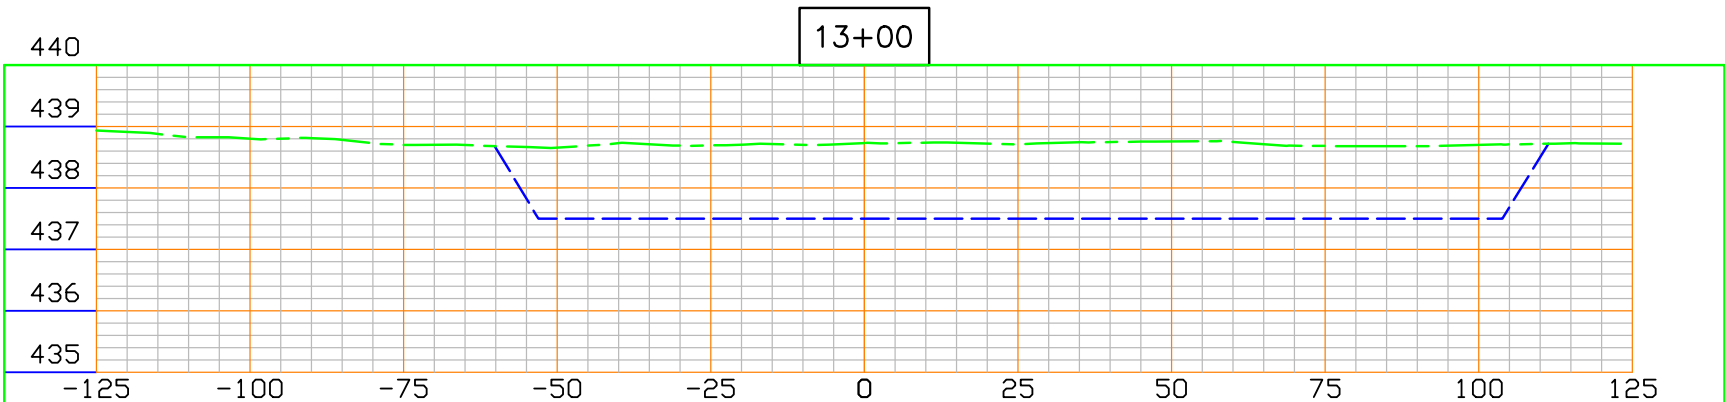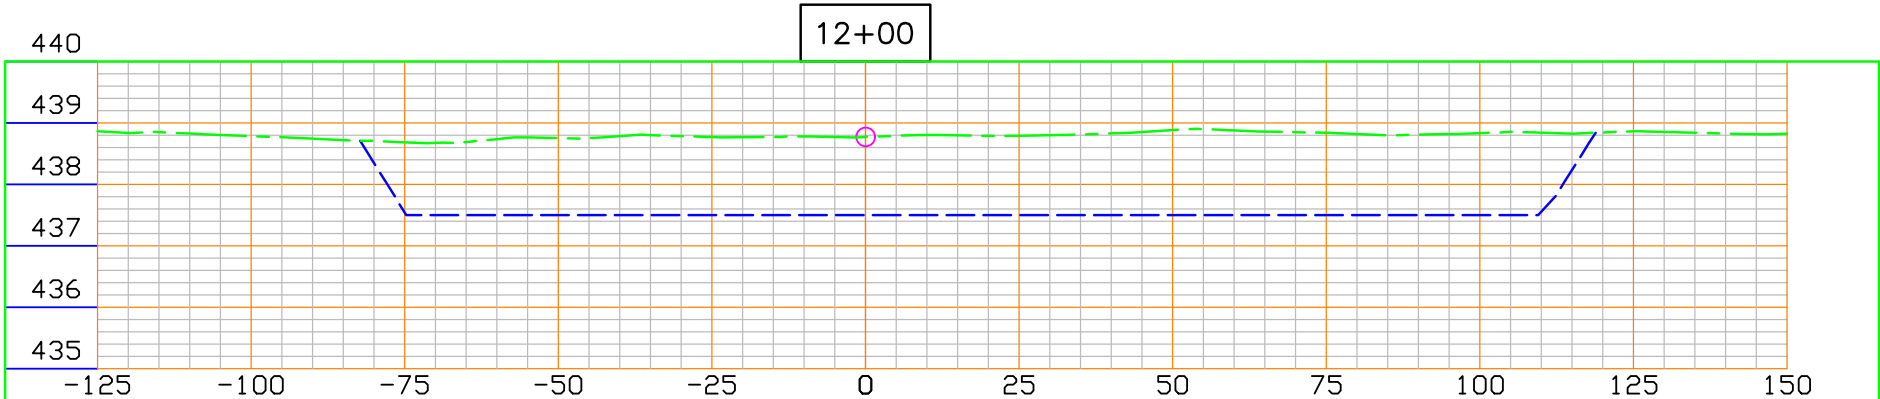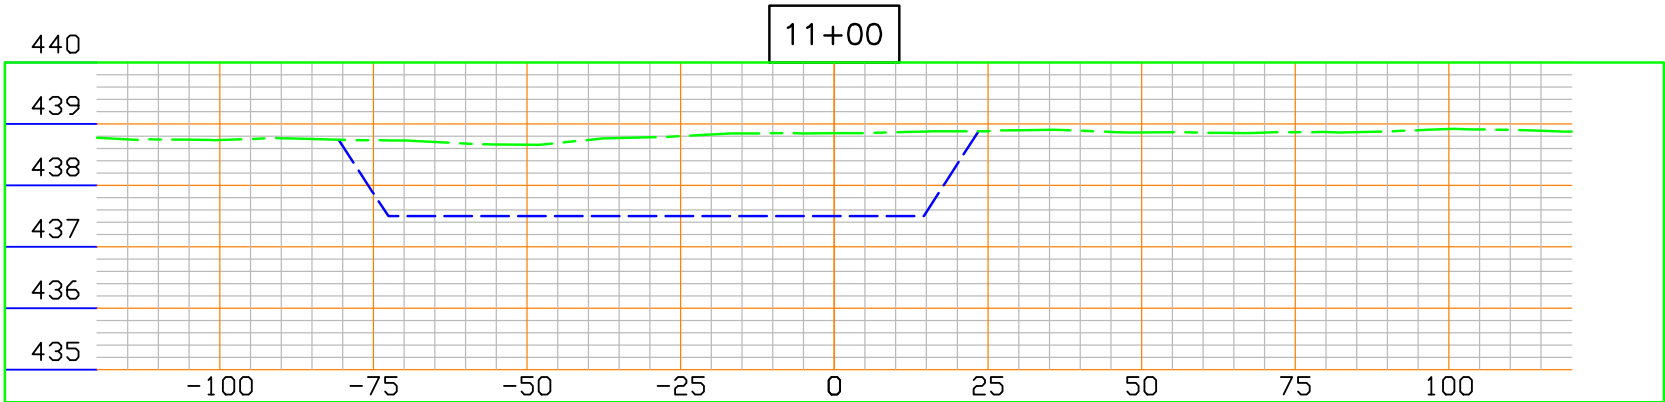

File No.	 United States Department of Agriculture	POOL AA X-SECTIONS (1) Daugherty Wetland	Designed <u>Kerry Bushue</u> <u>10/23/23</u> Date
Drawing No.			Drawn <u>Kerry Bushue</u> <u>10/23/23</u>
Sheet <u>###</u> of <u>.</u>			Checked <u>W.Dasenbrock 8.2025</u>
Natural Resources Conservation Service		York Twnshp, . Sec 27 T 9N R 11W Clark County County, IL.	Approved <u>W.Dasenbrock 8.2025</u>

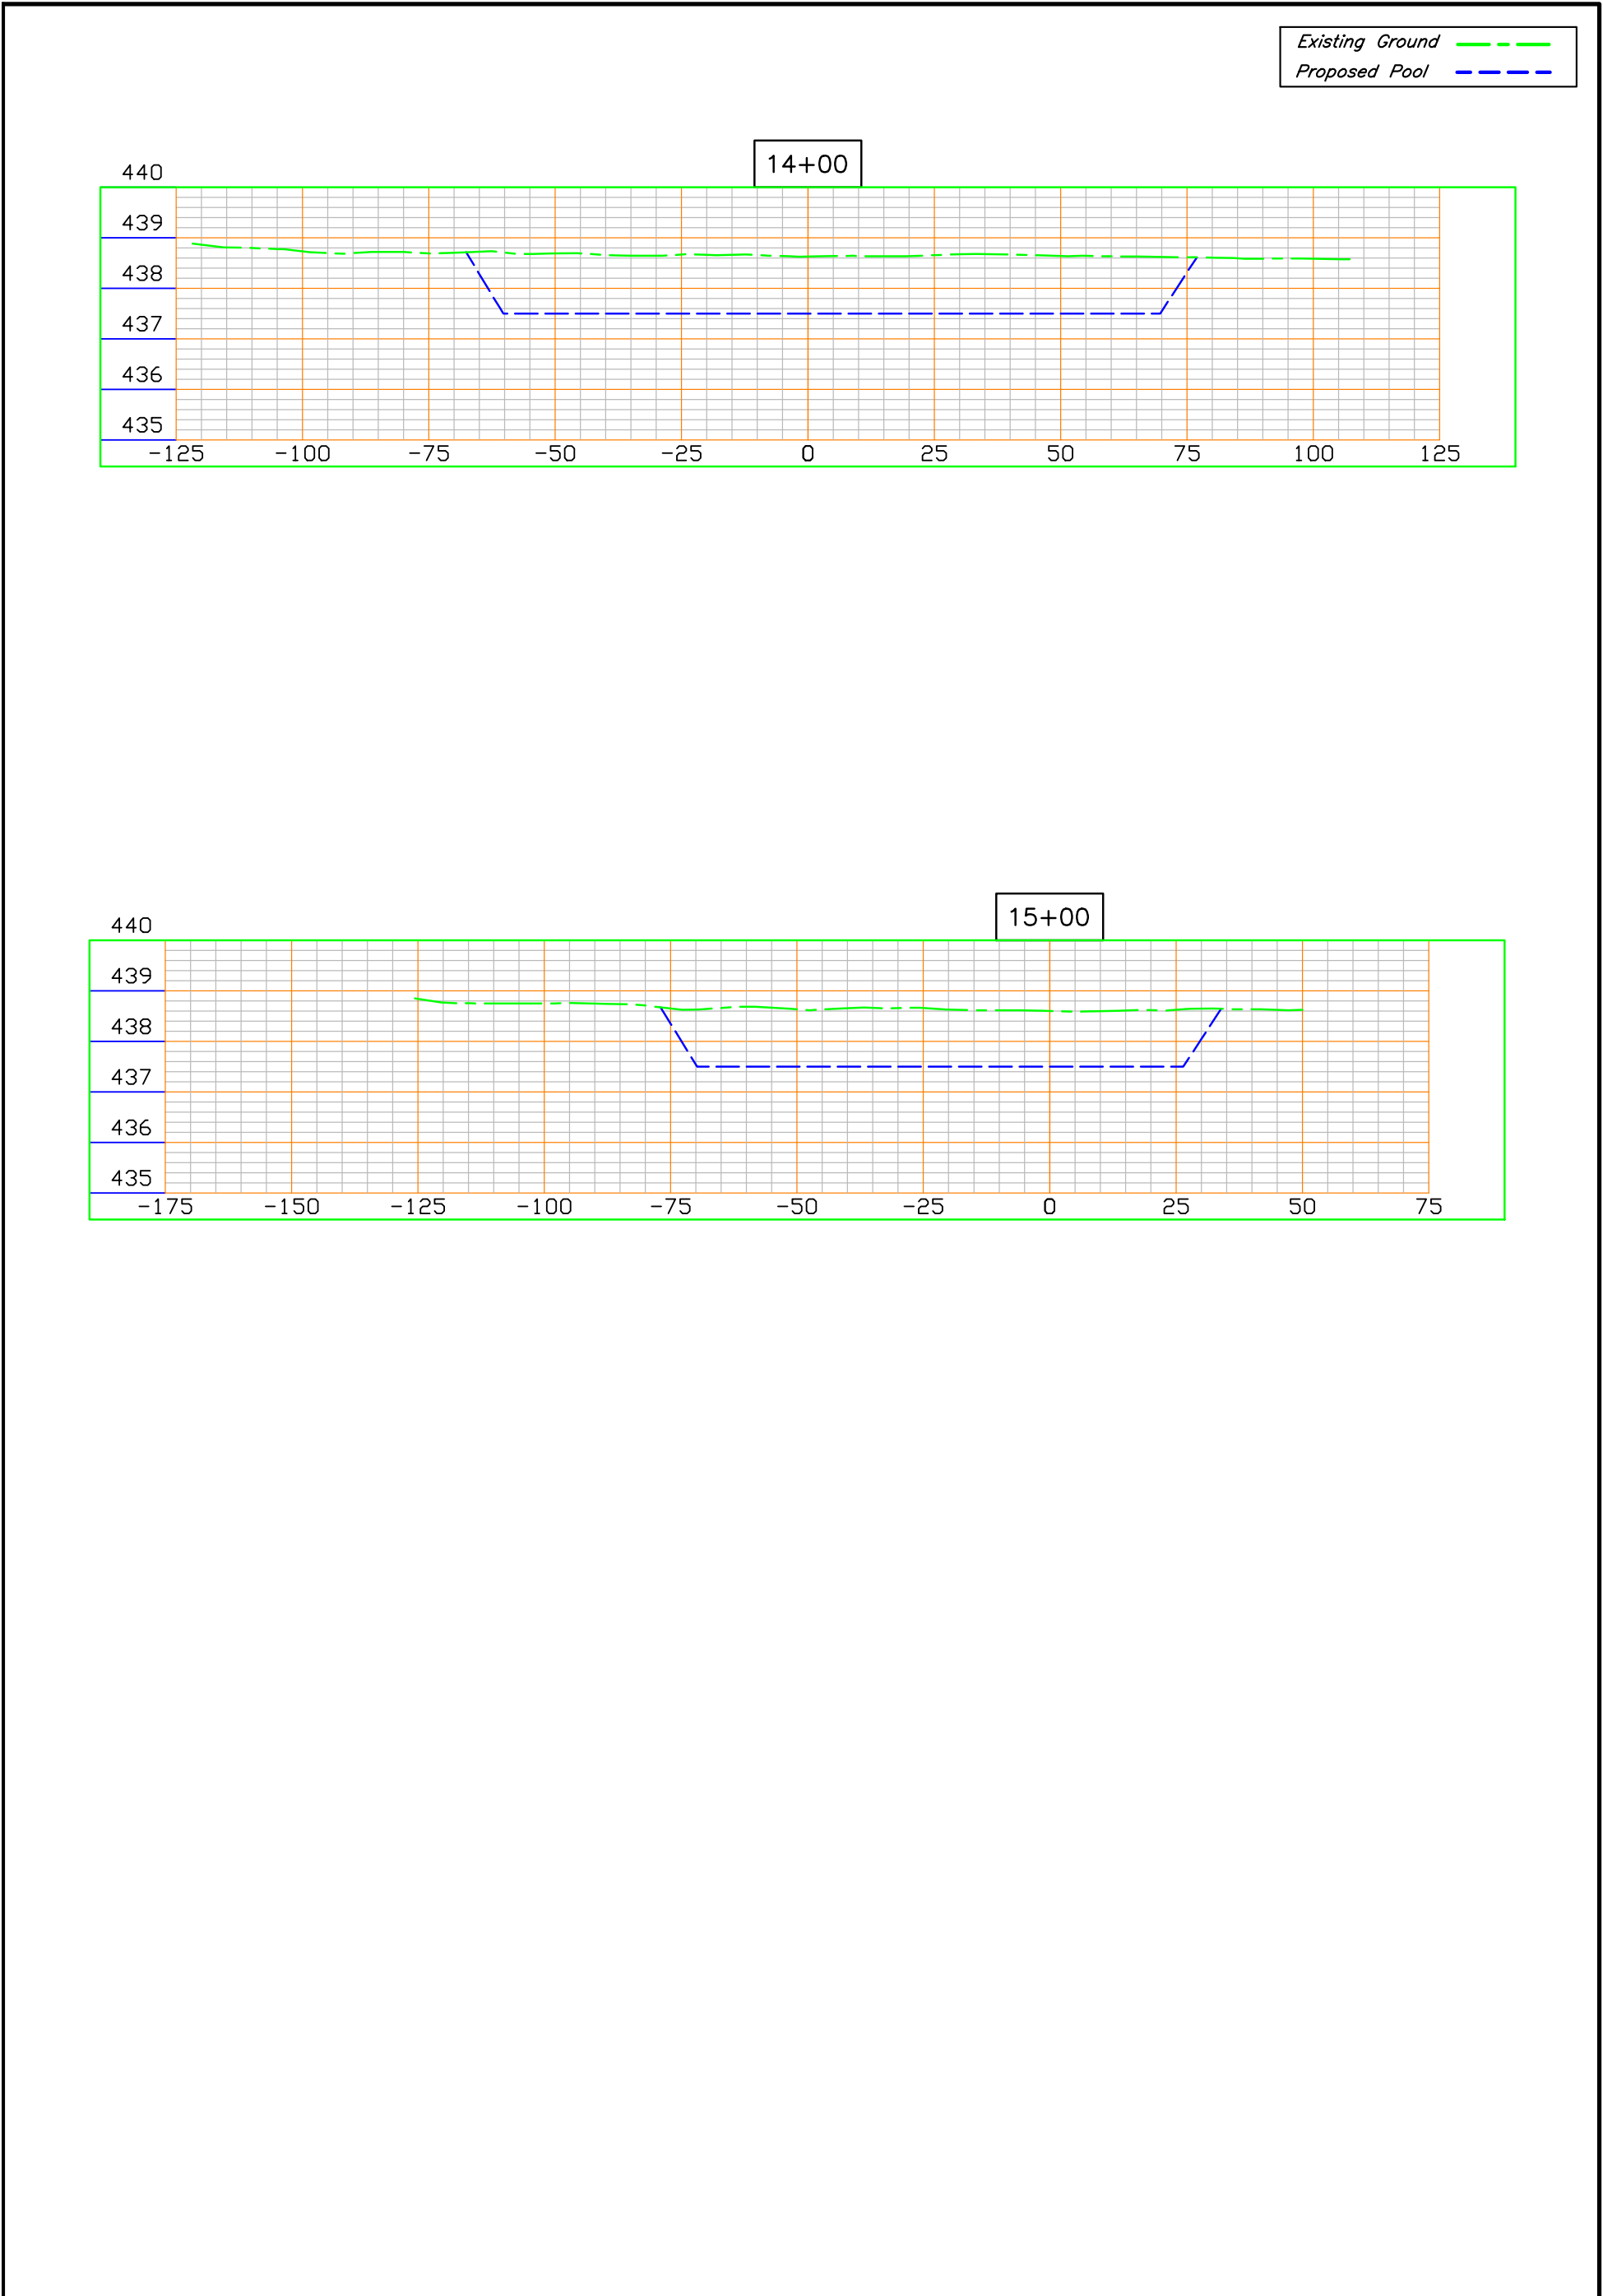

File No.	USDA United States Department of Agriculture Natural Resources Conservation Service	POOL AA X-SECTIONS (2) Daugherty Wetland	Date	
Drawing No.			Designed <u>Kerry Bushue</u> <u>10/23/23</u>	
			Drawn <u>Kerry Bushue</u> <u>10/23/23</u>	
			Checked <u>W.Dasenbrock 8.2025</u>	
Sheet <u>0000</u> of <u>0000</u>		York Twnshp, . Sec 27 T 9 N R 11 W Clark County County, IL.	Approved <u>W.Dasenbrock 8.2025</u>	


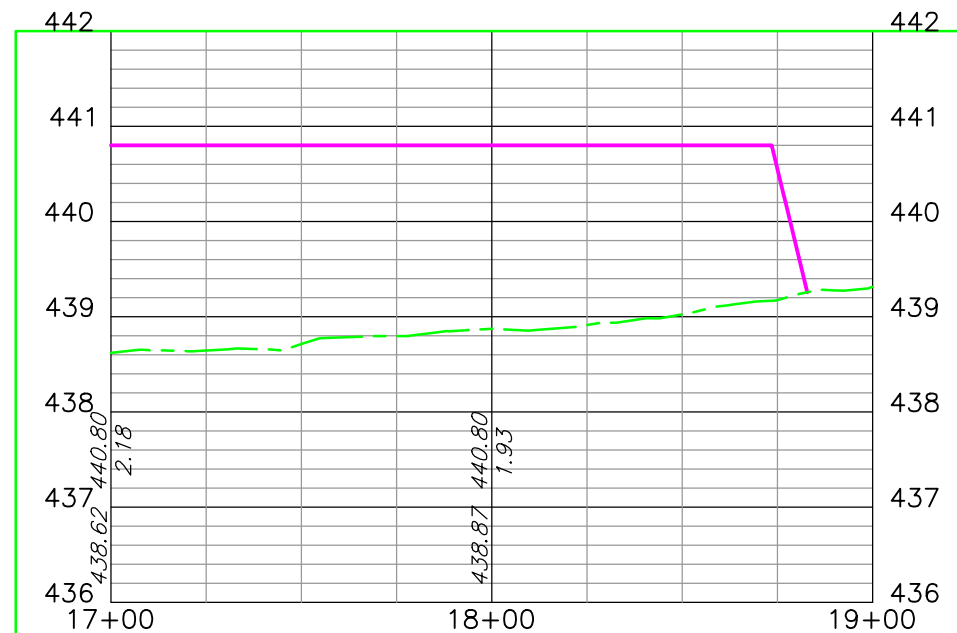
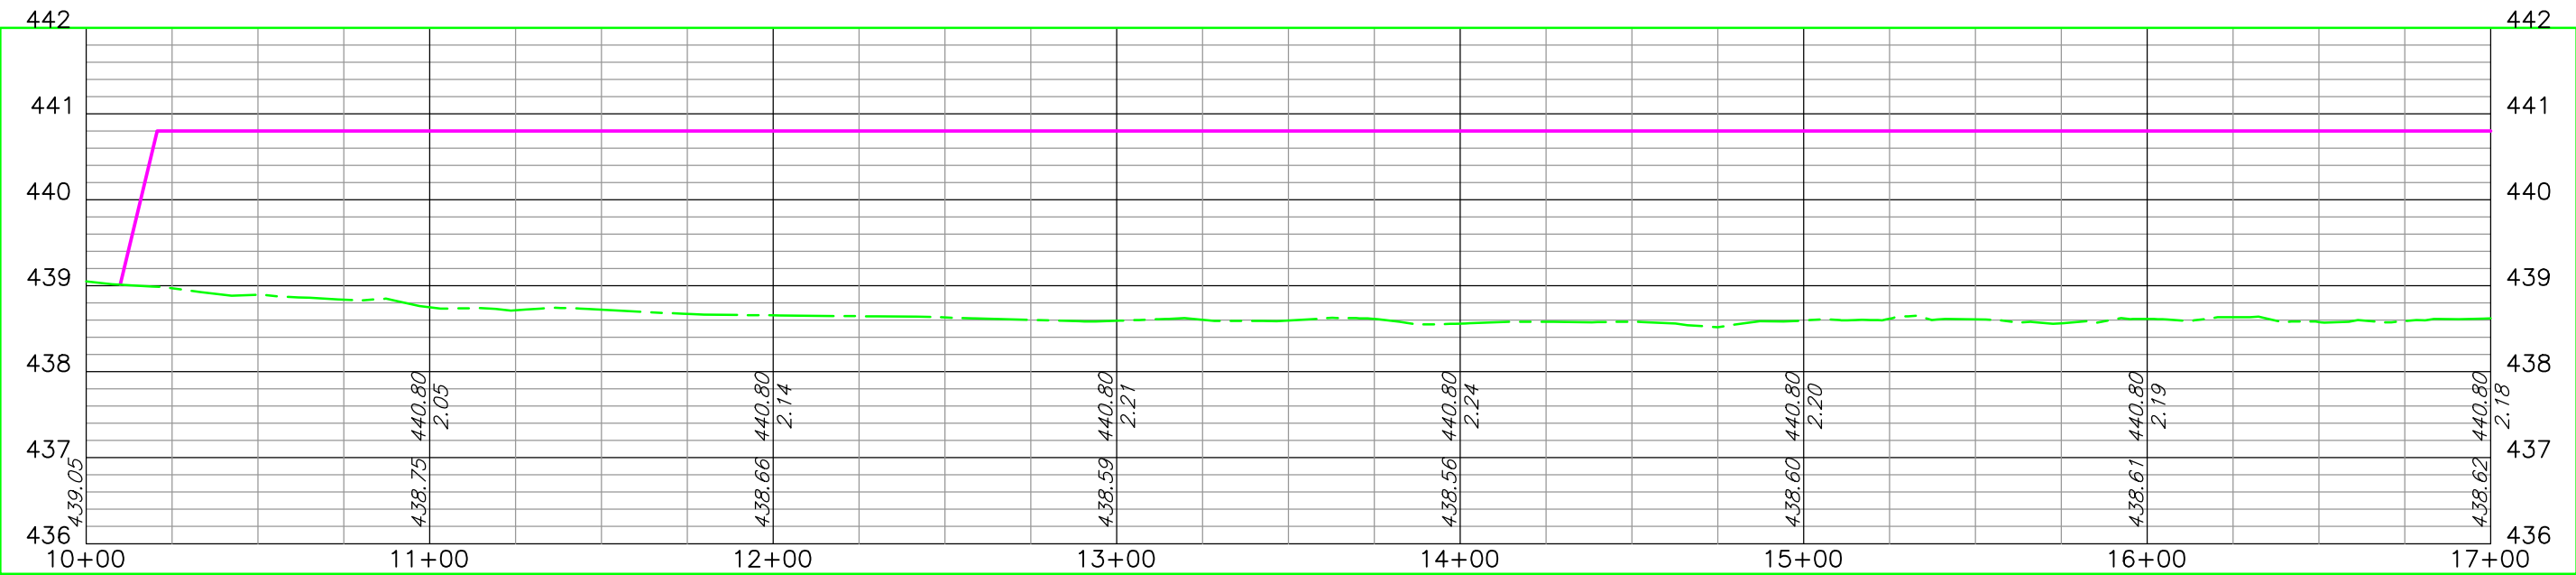


Designed Kerry Bushue 10/23/23
Drawn Kerry Bushue 10/23/23
Checked M. Daanbrock 8.20.25
Approved M. Daanbrock 8.20.25




HM1 PROFILE
Daugherty Wetland





File No. _____
Drawing No. _____
Sheet 11 of 48

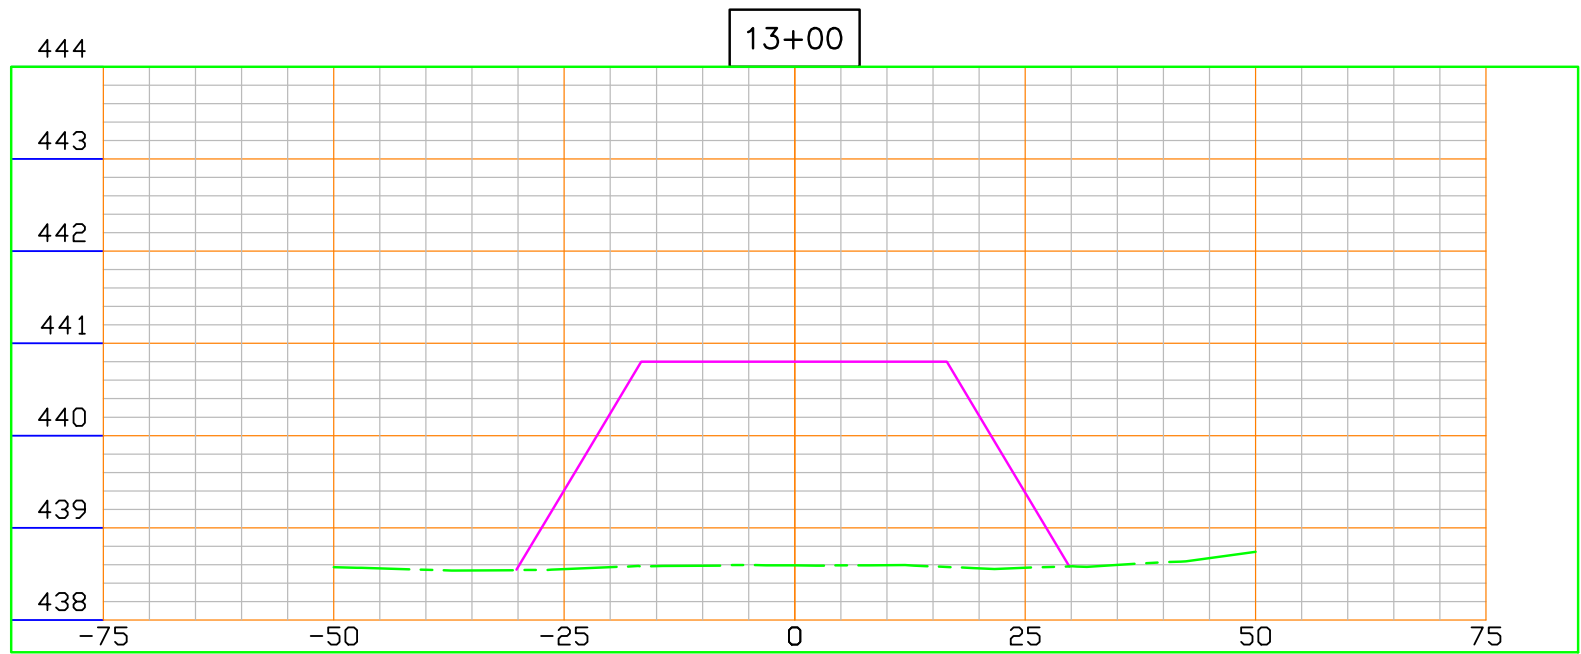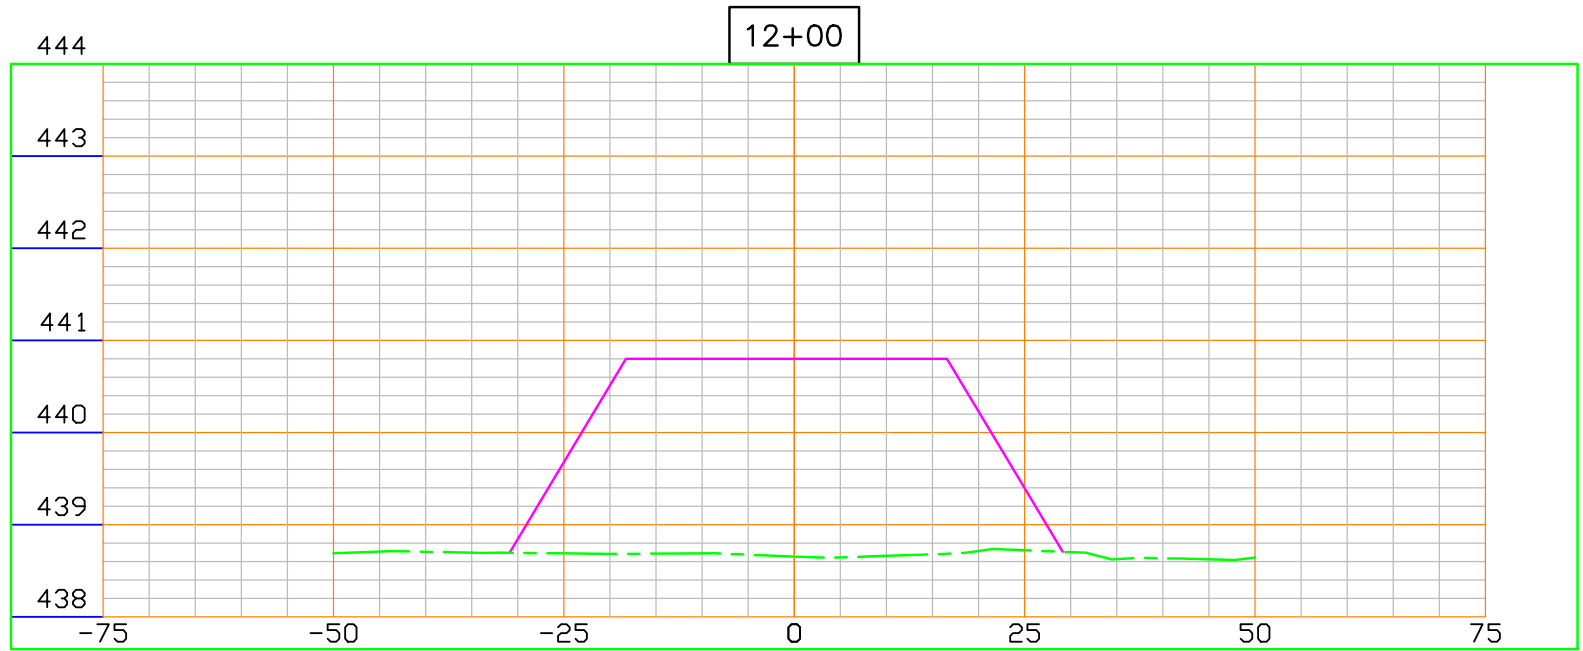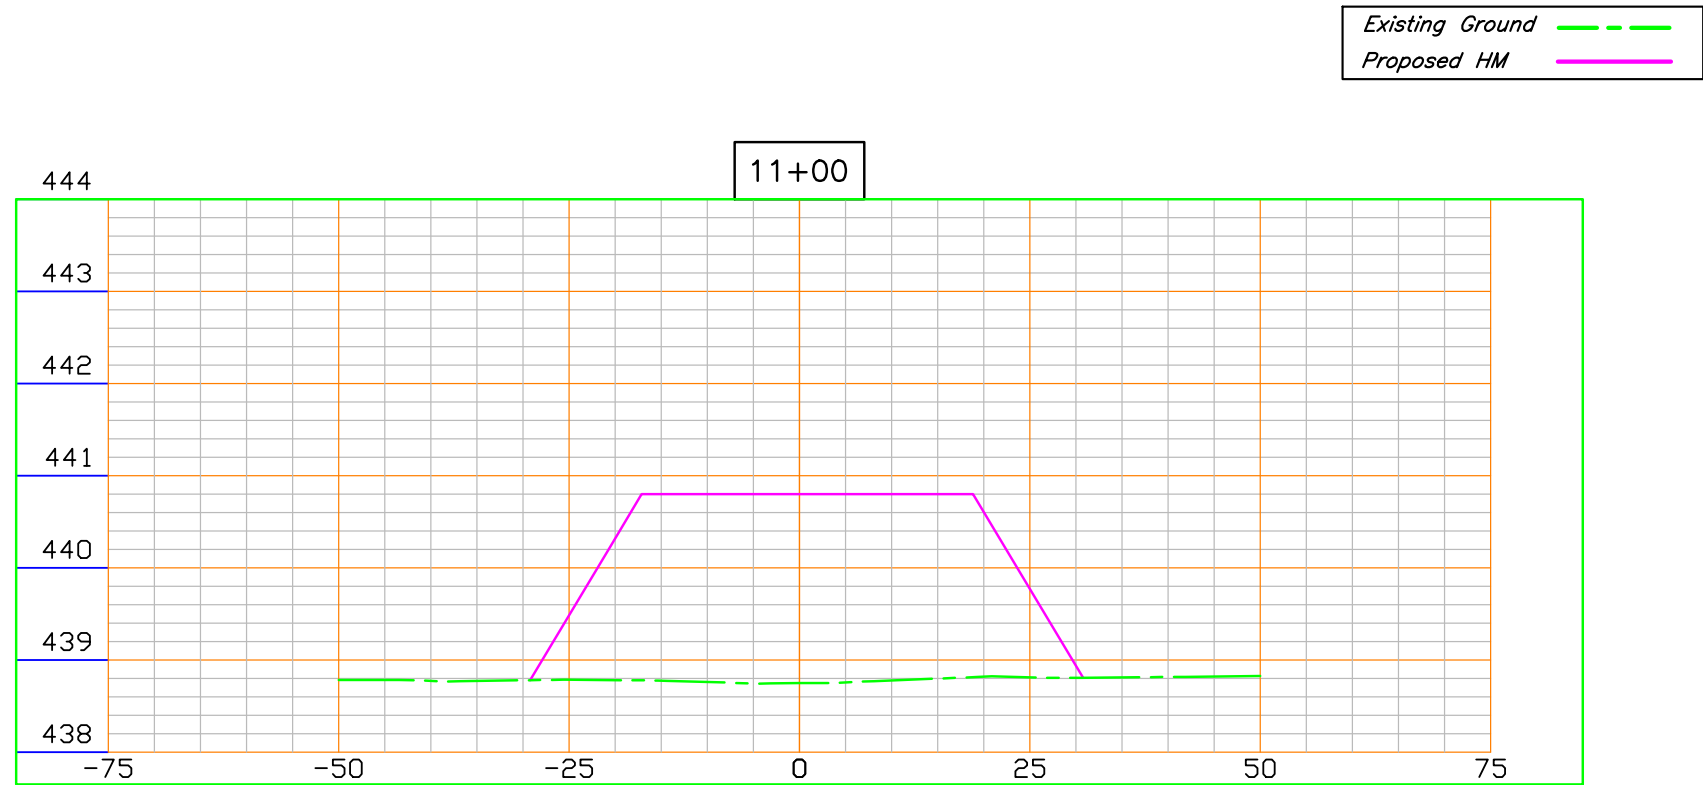


File No.	 United States Department of Agriculture	HM1 X-SECTIONS (1) Daugherty Wetland	Date Designed <u>Kerry Bushue</u> <u>10/23/23</u>				
Drawing No. -----			Drawn <u>Kerry Bushue</u> <u>10/23/23</u>				
Sheet <u>11</u> of <u>48</u>			Checked <u>M. Dasenbrock</u> <u>8.2025</u>				
Natural Resources Conservation Service		York Twnshp, .	Sec 27	T 9 N	R 11 W	Clark County County, IL.	Approved <u>M. Dasenbrock</u> <u>8.2025</u>

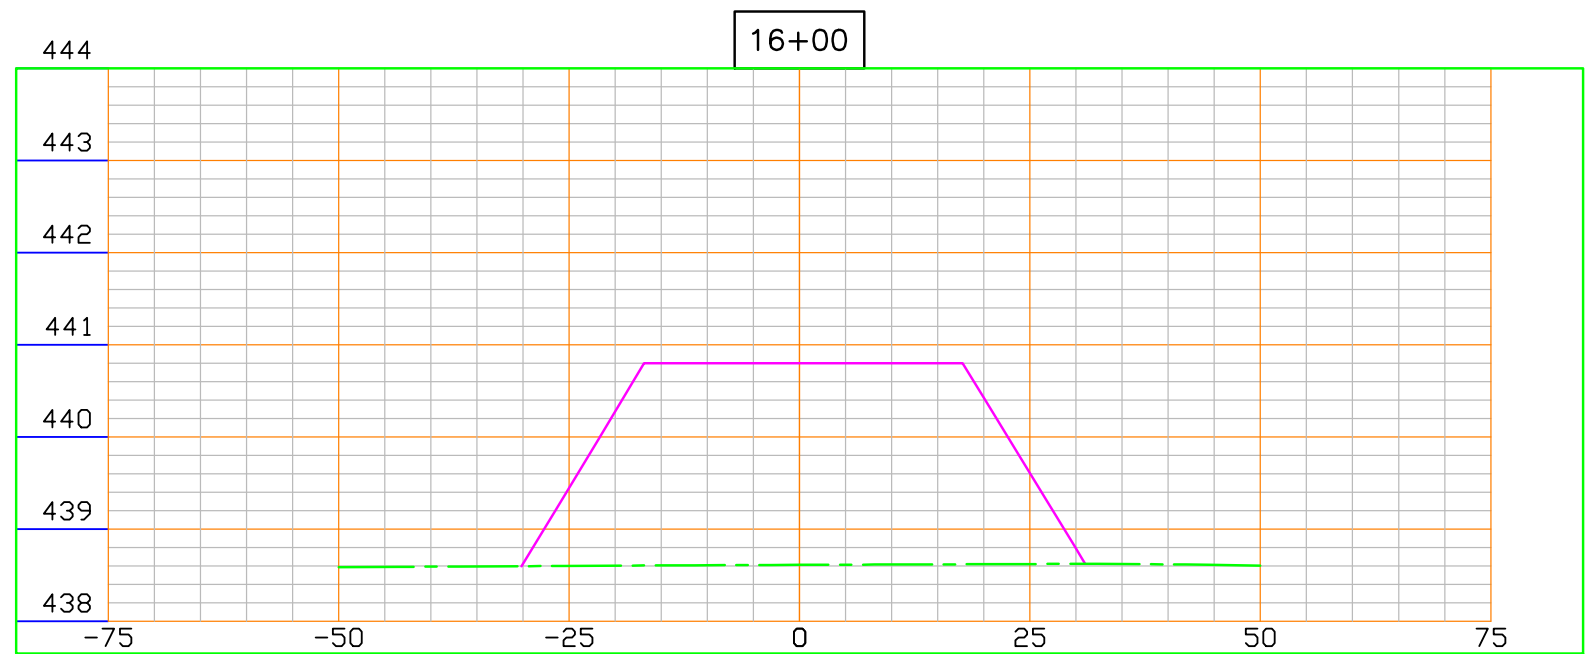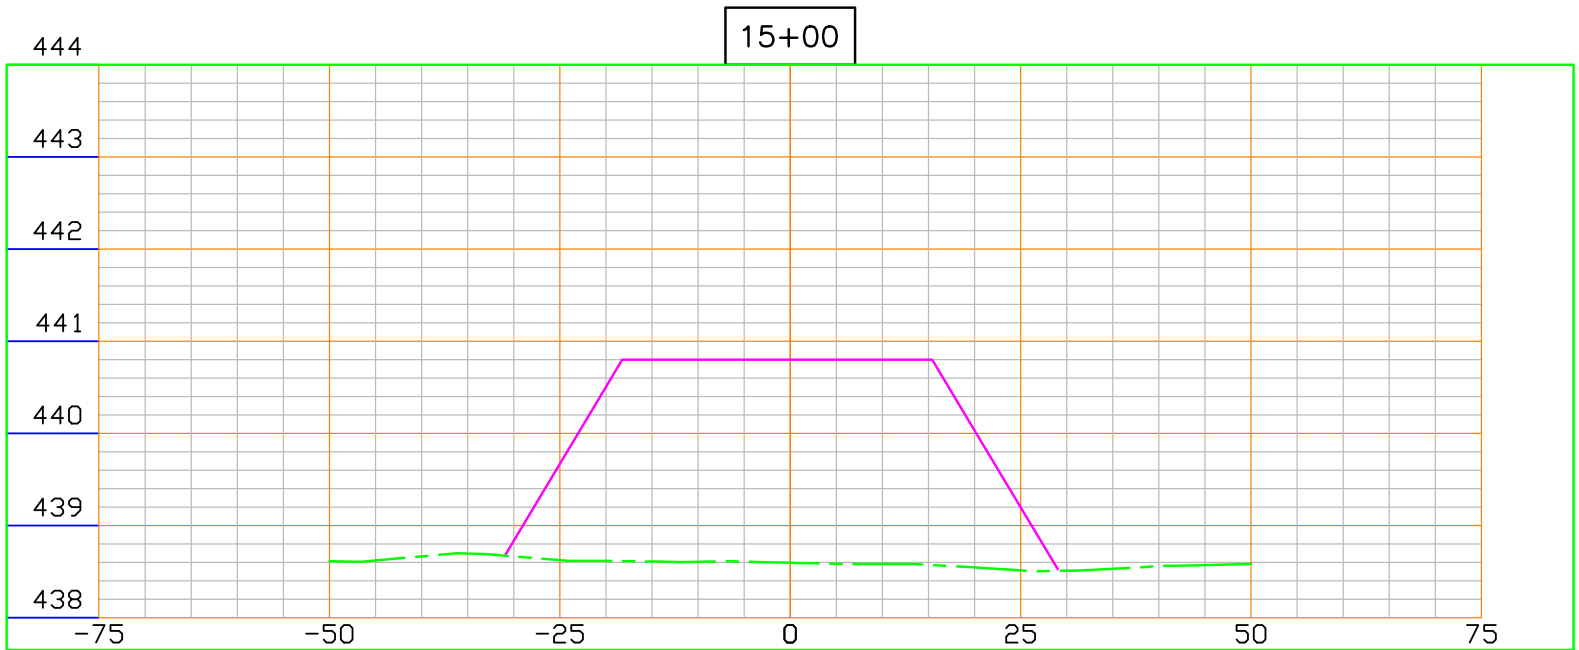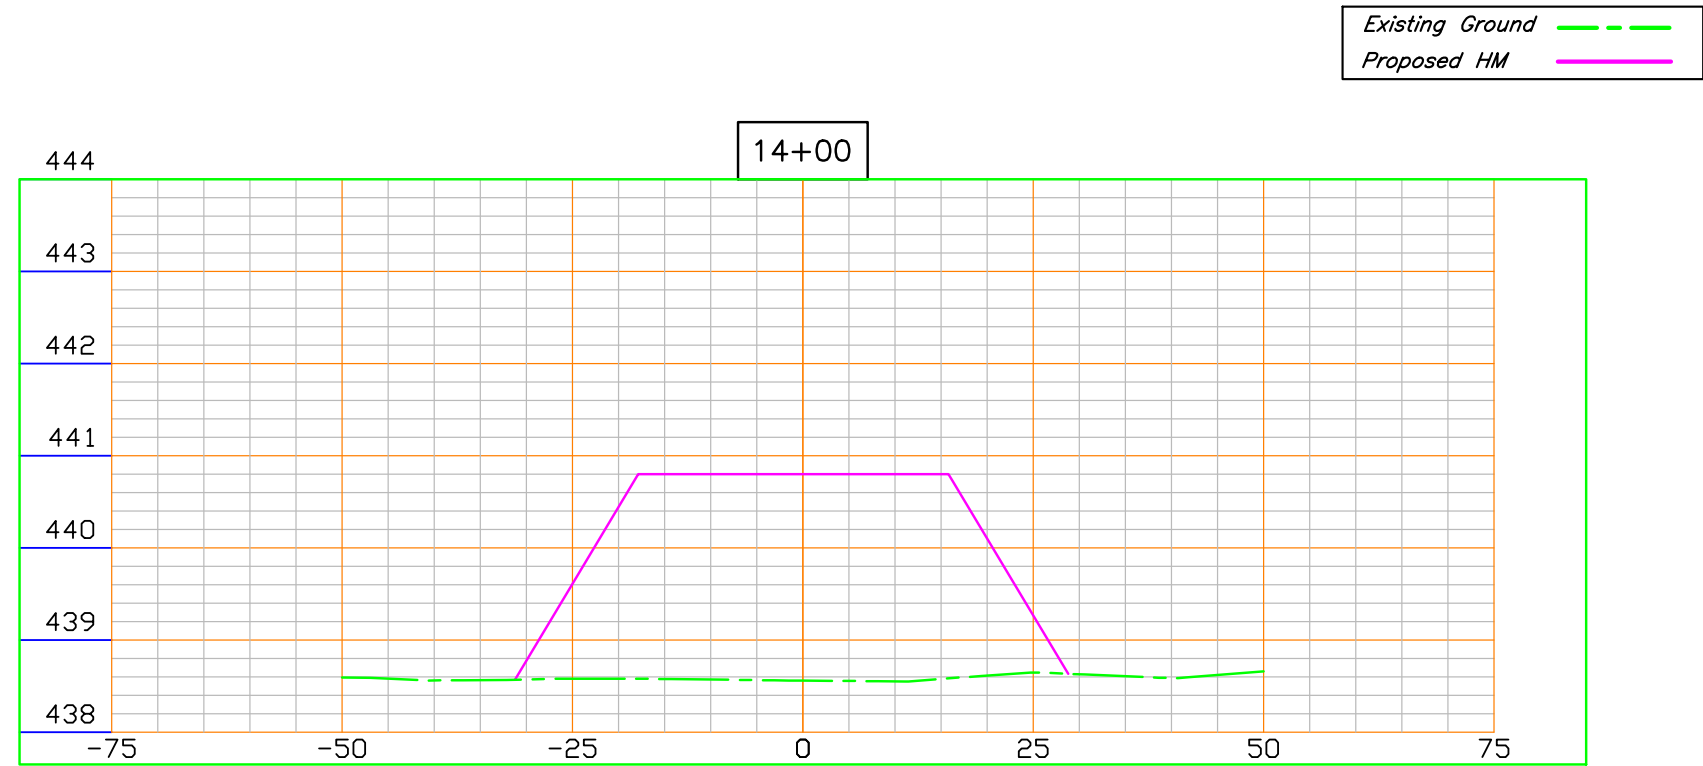

File No.	 United States Department of Agriculture Natural Resources Conservation Service	HM1 X-SECTIONS (2) Daugherty Wetland	Designed <u>Kerry Bushue</u> <u>10/23/23</u>	
Drawing No.			Drawn <u>Kerry Bushue</u> <u>10/23/23</u>	
Sheet <u>11</u> of <u>48</u>			Checked <u>W. Dasenbrock 8.2025</u>	
York Twnshp, .		Sec 27 T 9 N R 11 W	Clark County County, IL.	Approved <u>W. Dasenbrock 8.2025</u>

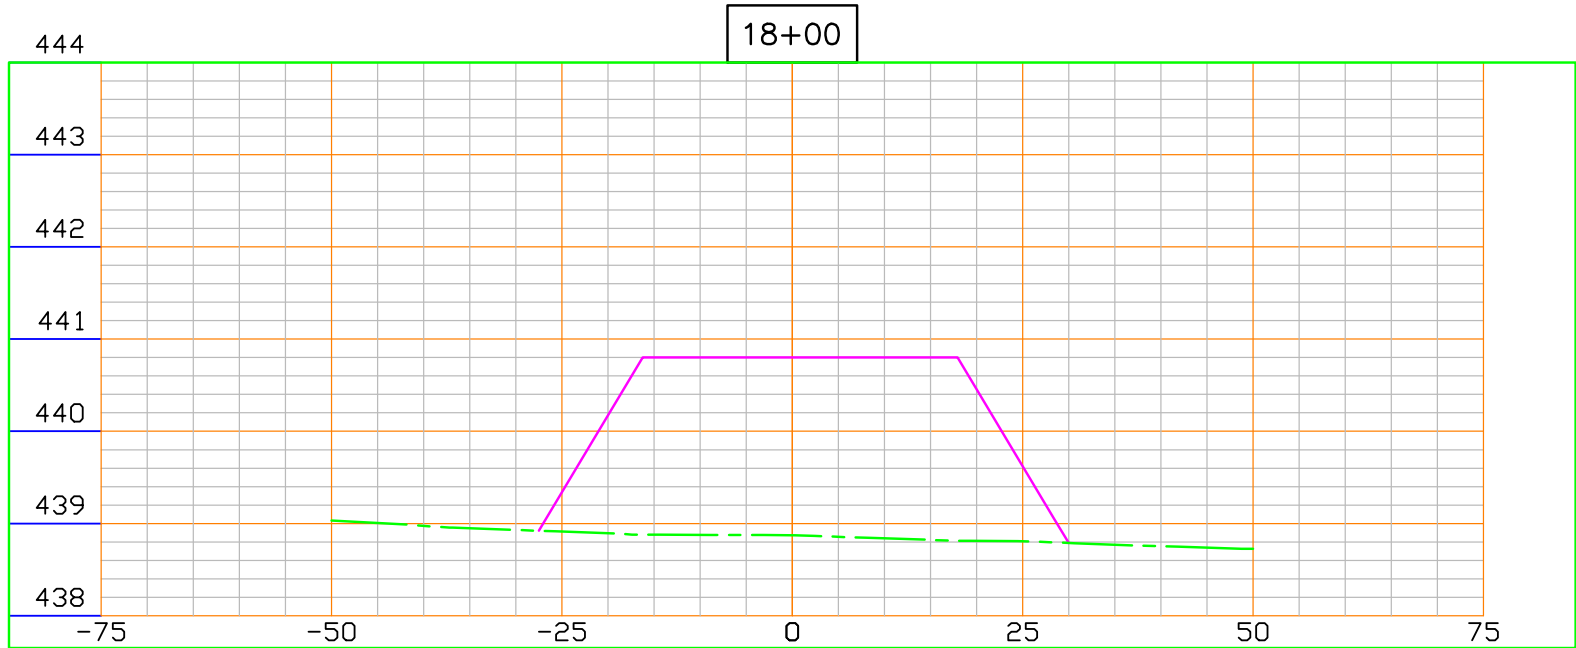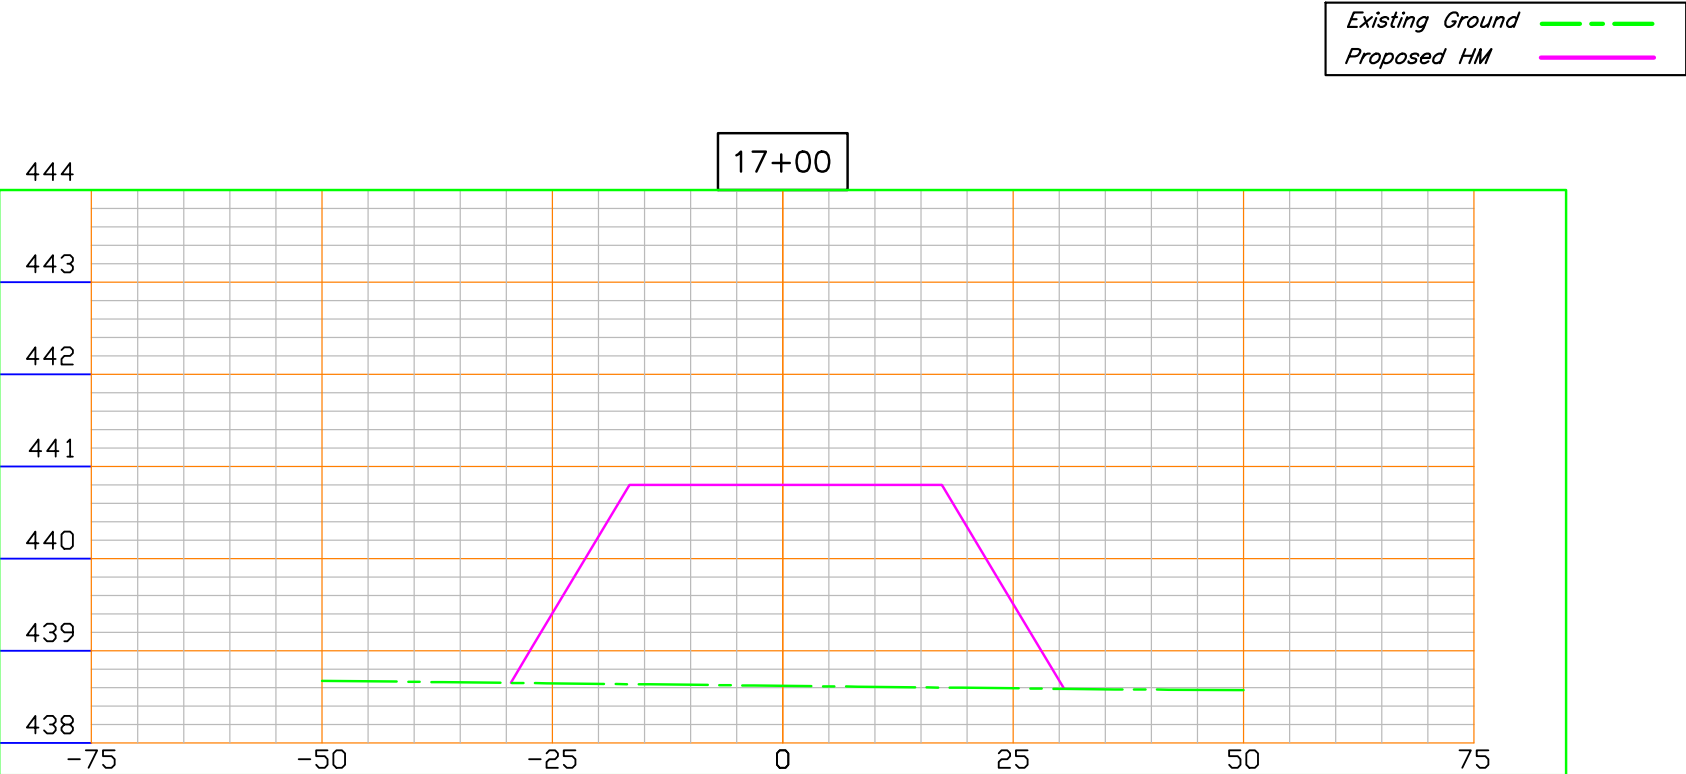

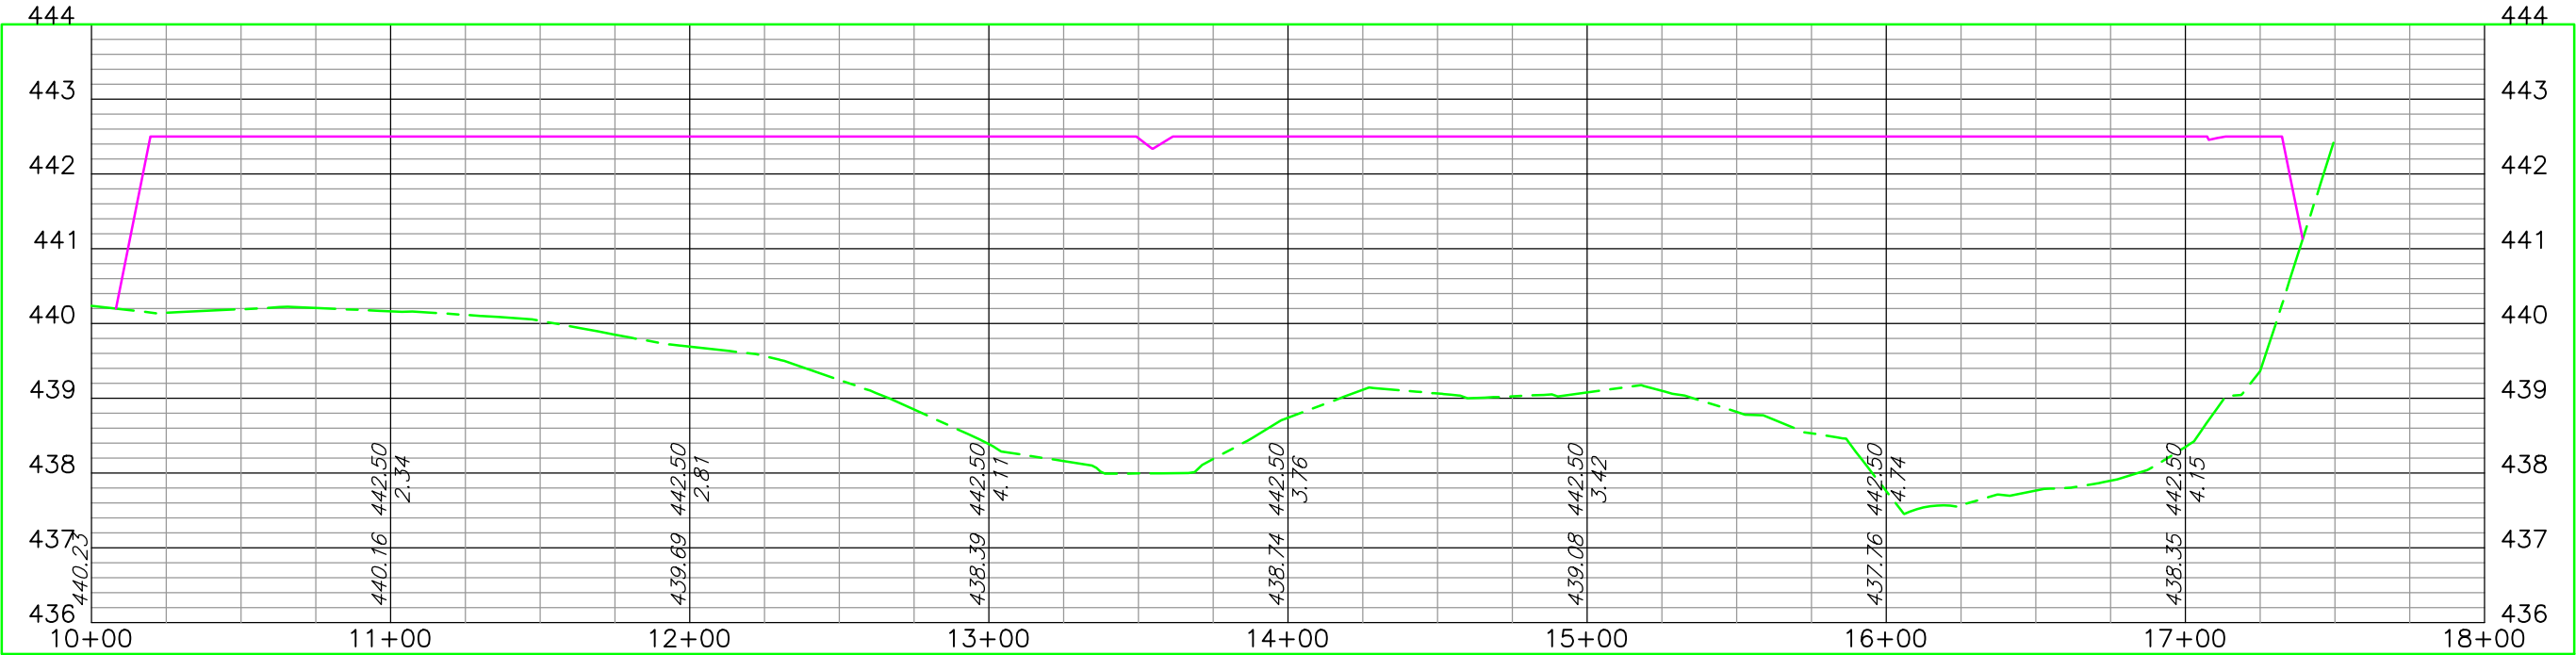




Designed Kerry Bushue 10/23/23
Drawn Kerry Bushue 10/23/23
Checked M. Daanbroek 8/2025
Approved M. Daanbroek 8/2025

York Twnshp, . Sec27 T 9N R 11W Clark County, IL
HM3 PROFILE
Daugherty Wetland







File No. _____
Drawing No. _____
Sheet 11 of 11

Existing Ground
Proposed HM

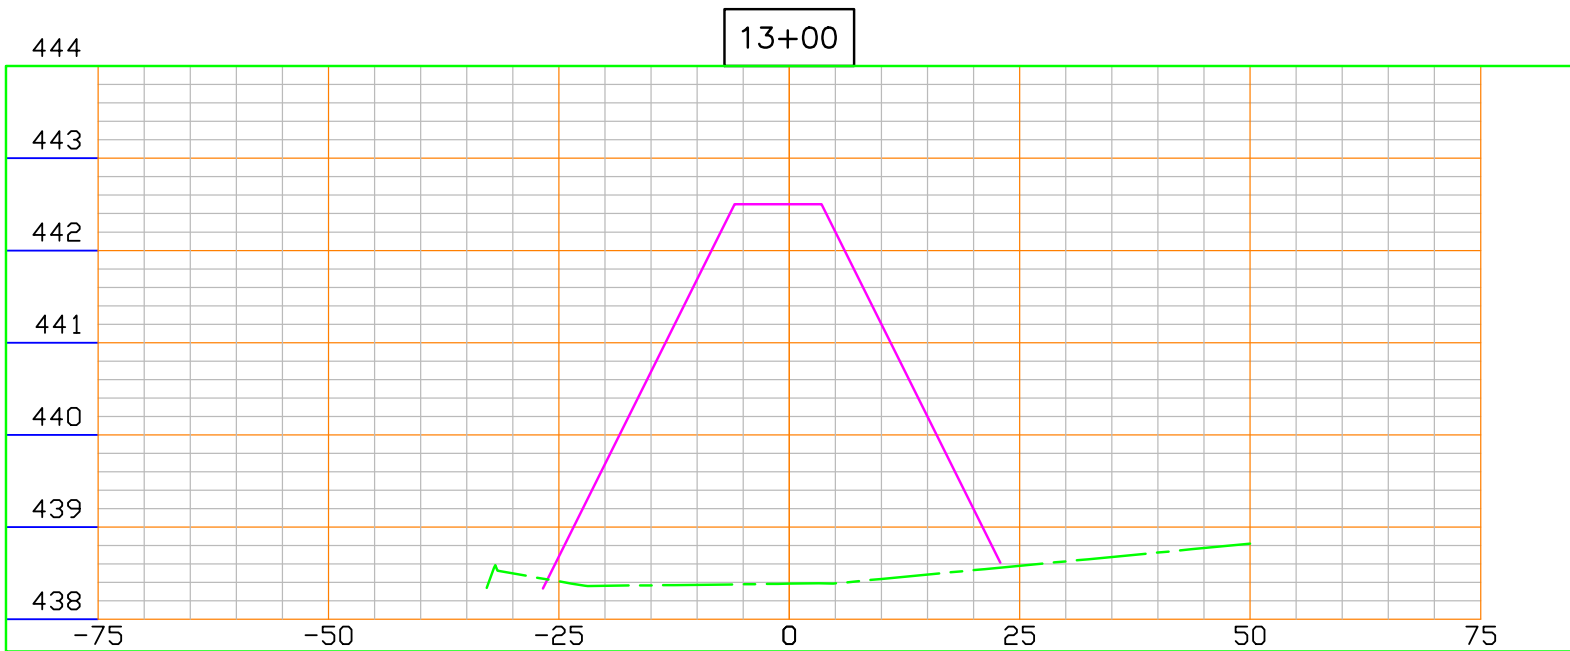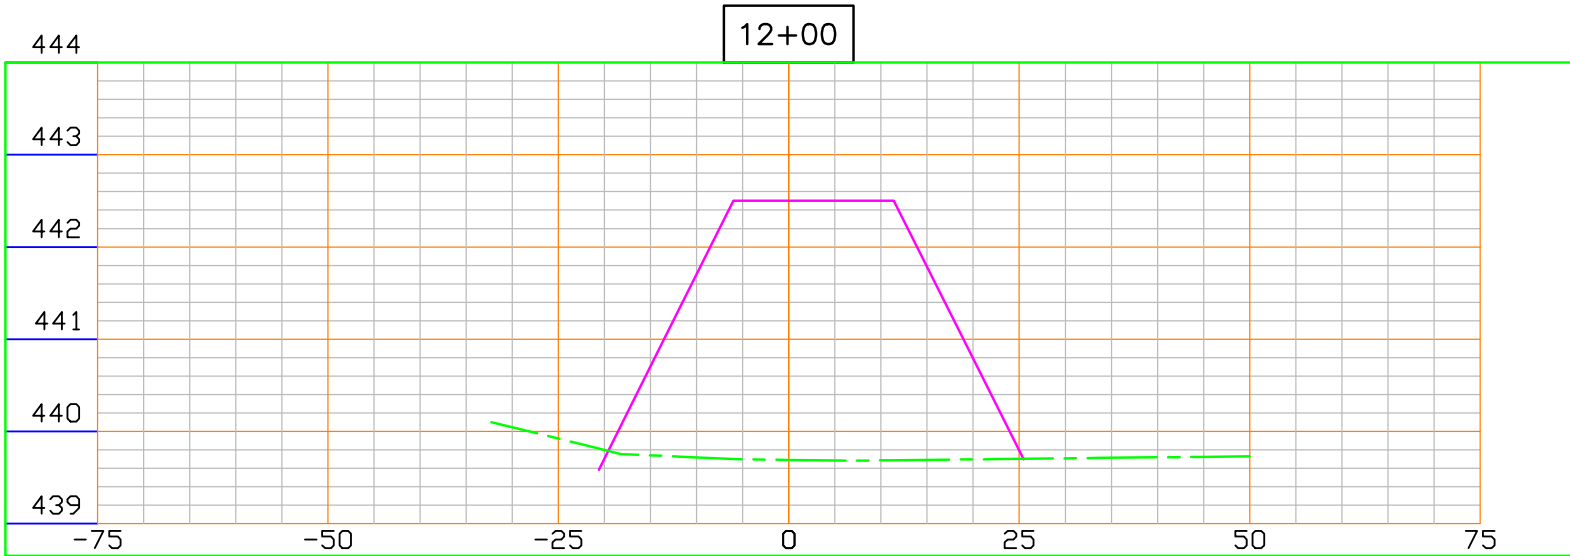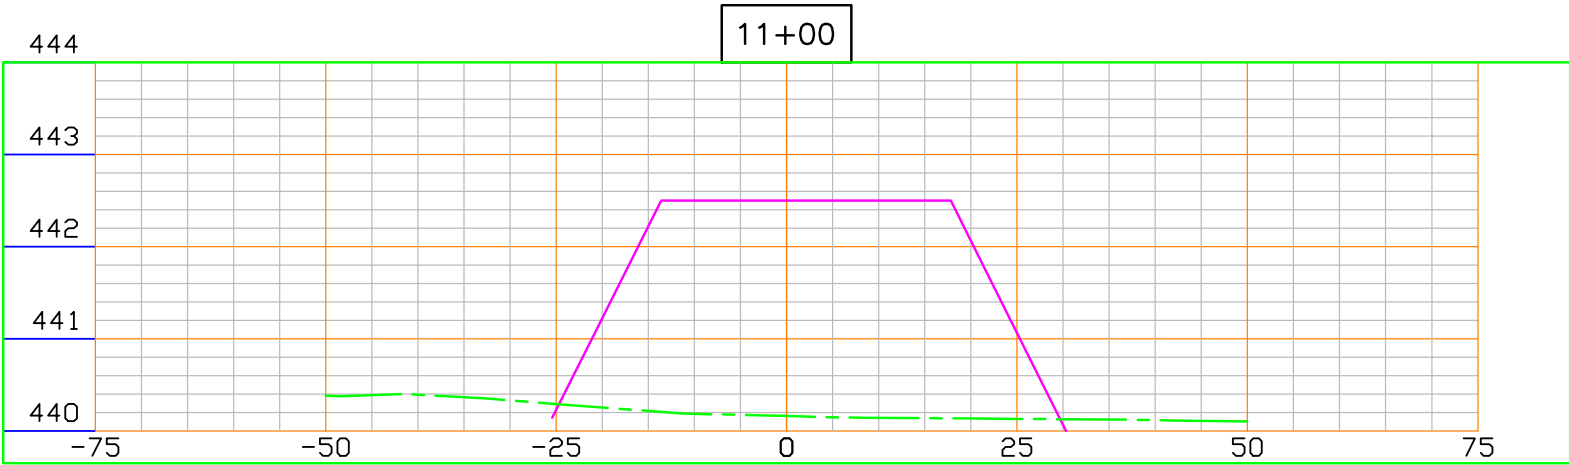


File No.	 United States Department of Agriculture Natural Resources Conservation Service	HM3 X-SECTIONS (1) Daugherty Wetland	Designed <u>Kerry Bushue</u> <u>10/23/23</u>
Drawing No.			Drawn <u>Kerry Bushue</u> <u>10/23/23</u>
Sheet <u>11</u> of <u>11</u>			Checked <u>W.Dasenbrock 8.2025</u> Approved <u>W.Dasenbrock 8.2025</u>
		York Twnshp, . Sec 27 T 9N R 11W Clark County County, IL.	

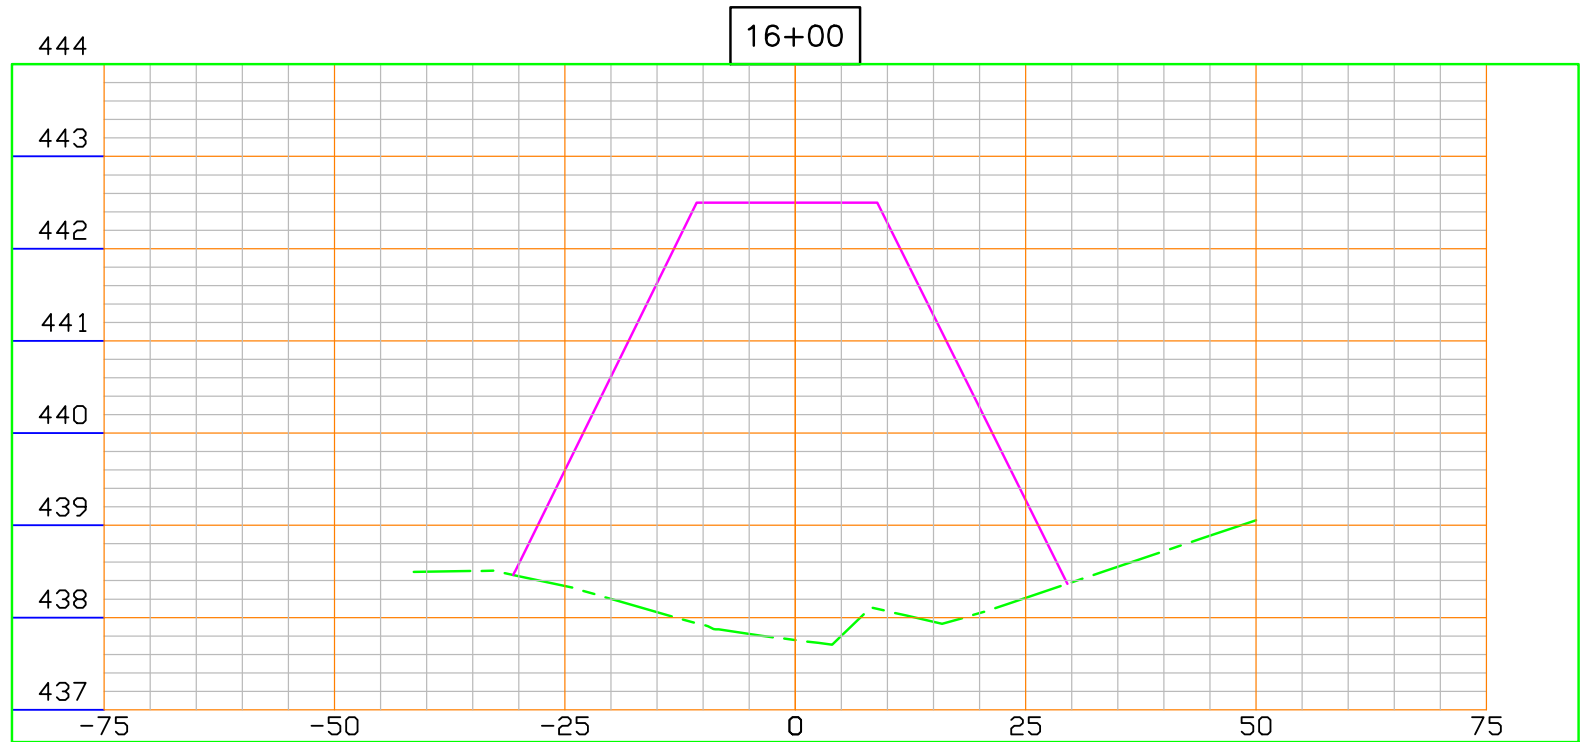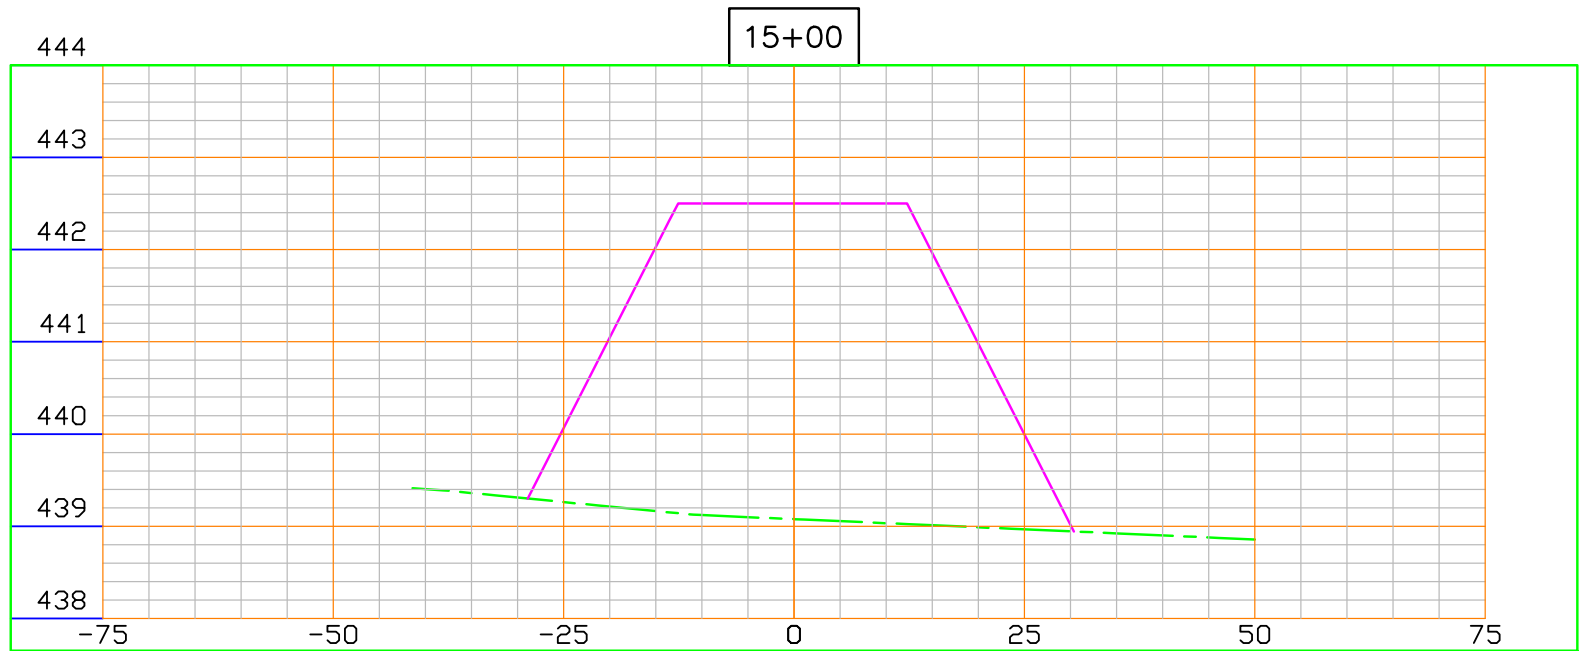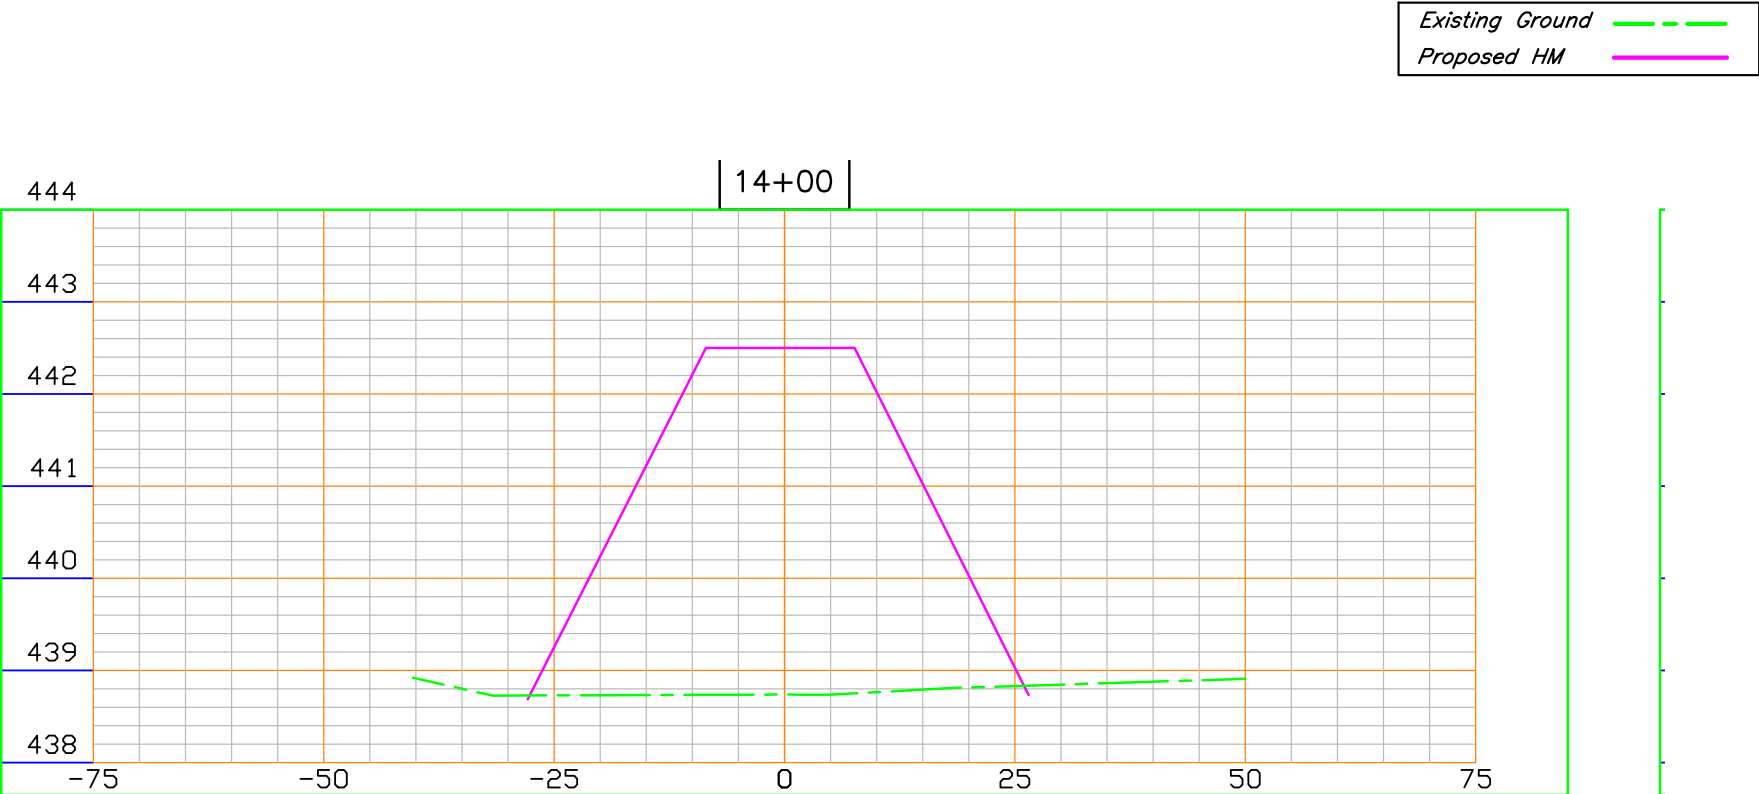

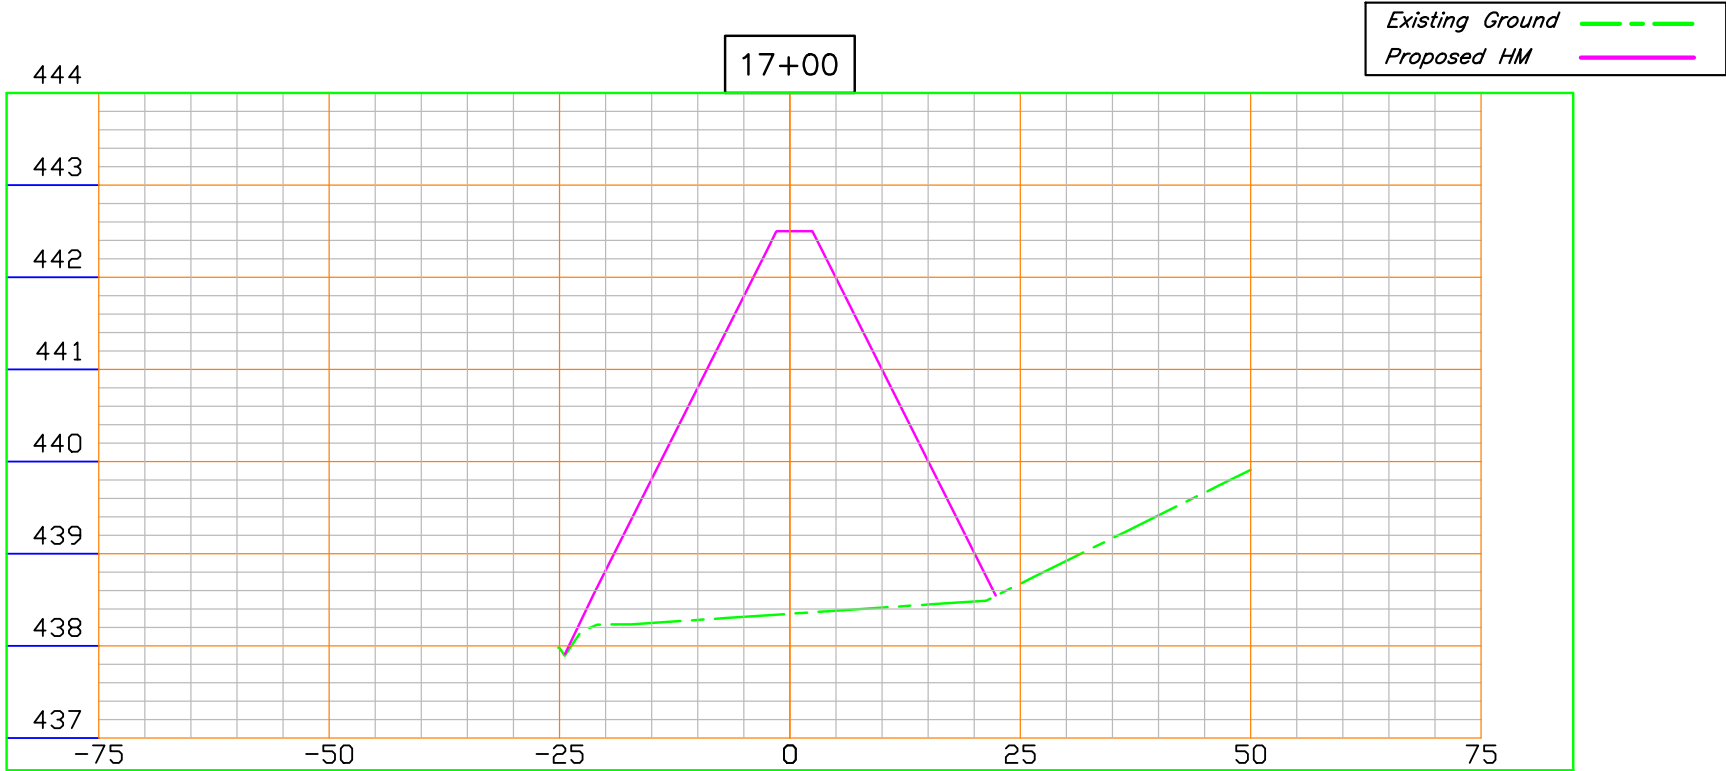

File No.	 United States Department of Agriculture Natural Resources Conservation Service	HM3 X-SECTIONS (3) Daugherty Wetland	Designed <u>Kerry Bushue</u> <u>10/23/23</u> Date
Drawing No. ----			Drawn <u>Kerry Bushue</u> <u>10/23/23</u>
Sheet <u>17</u> of <u>48</u>			Checked <u>W. Dassenbrock 8.2025</u> Approved <u>W. Dassenbrock 8.2025</u>
		York Twnshp, . Sec 27 T 9 N R 11 W Clark County County, IL.	

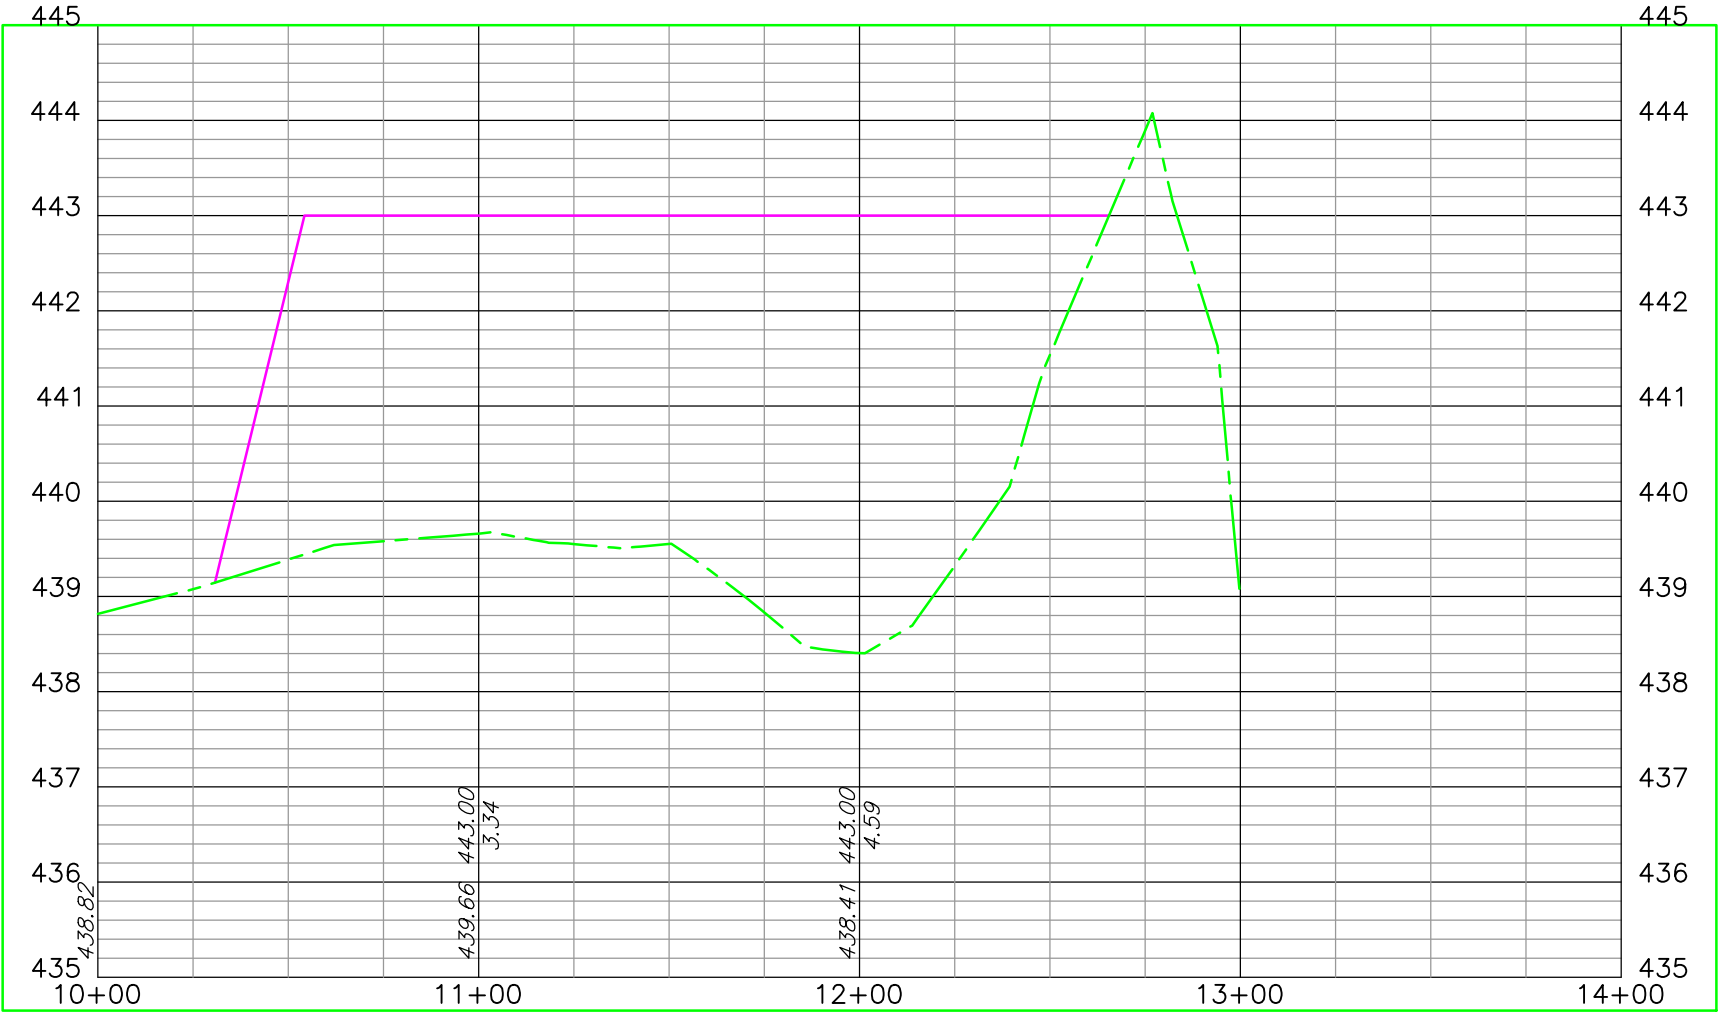




Existing Ground
Proposed HM

Designed Kerry Bushue 10/23/23
Drawn Kerry Bushue 10/23/23
Checked M. Dasenbrock 8/20/25
Approved M. Dasenbrock 8/20/25


HM3A PROFILE
Daugherty Wetland



File No.
Drawing No.
Sheet ### of ###

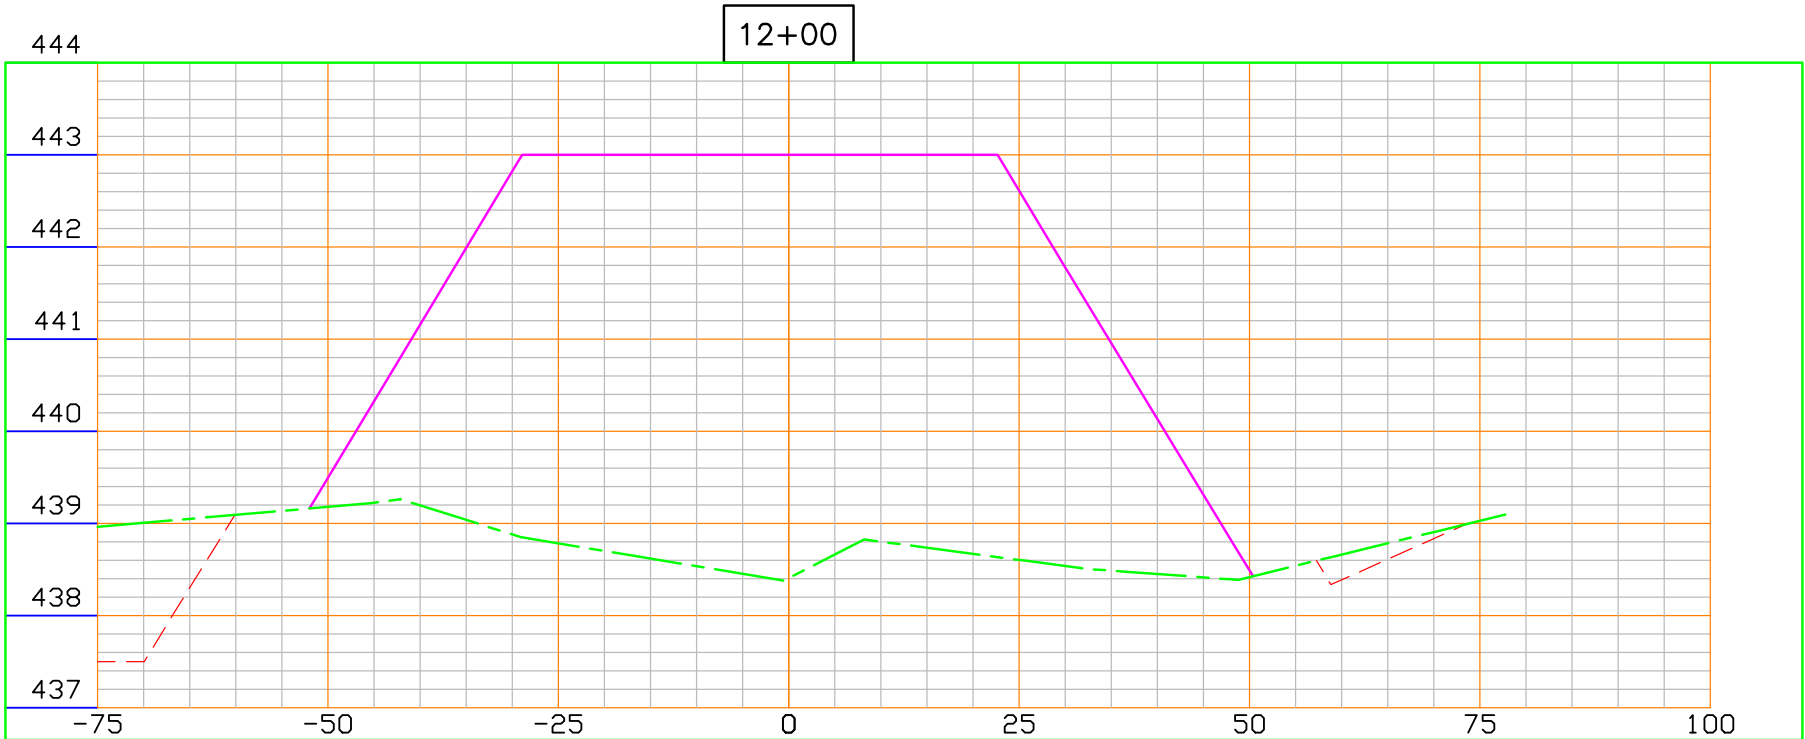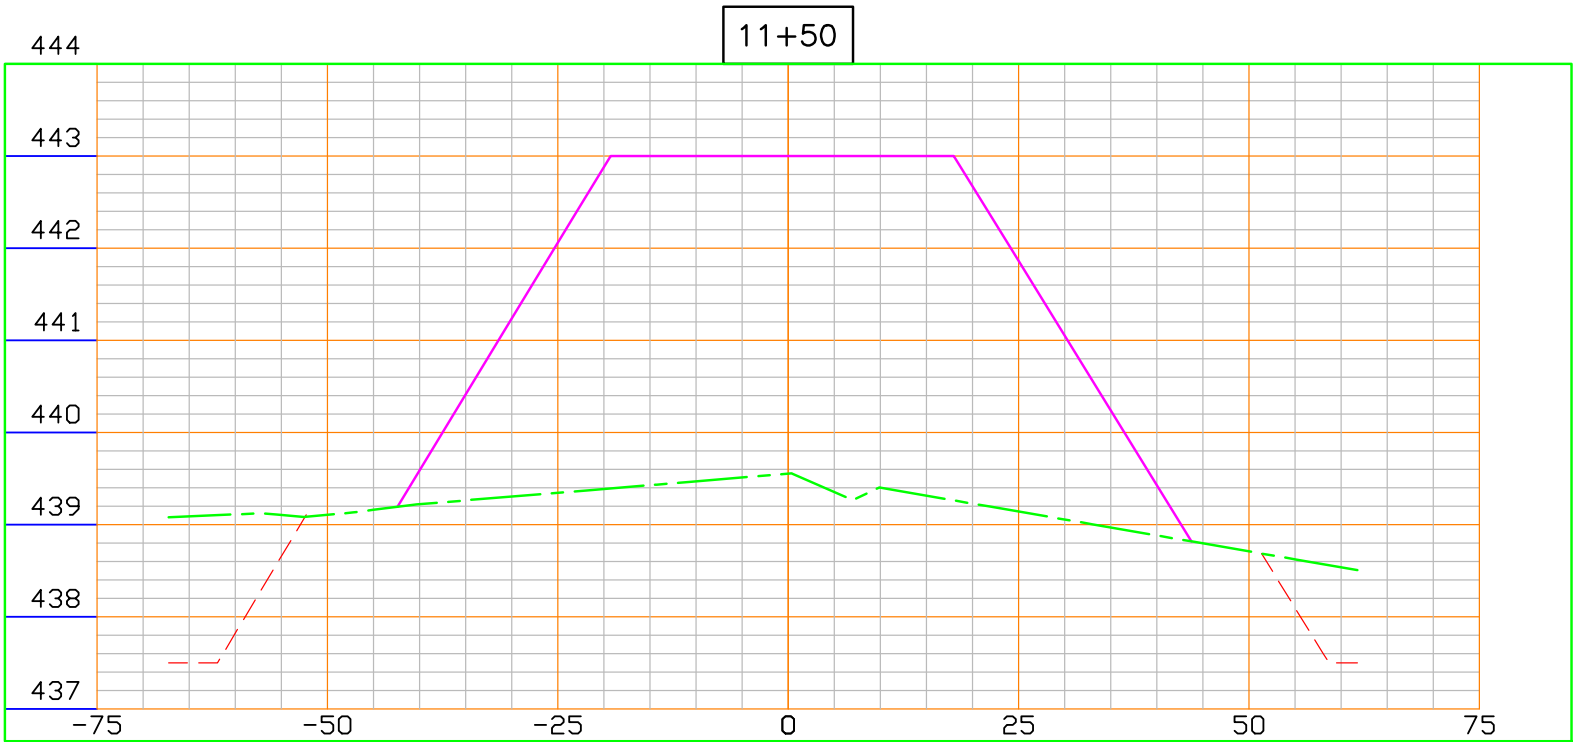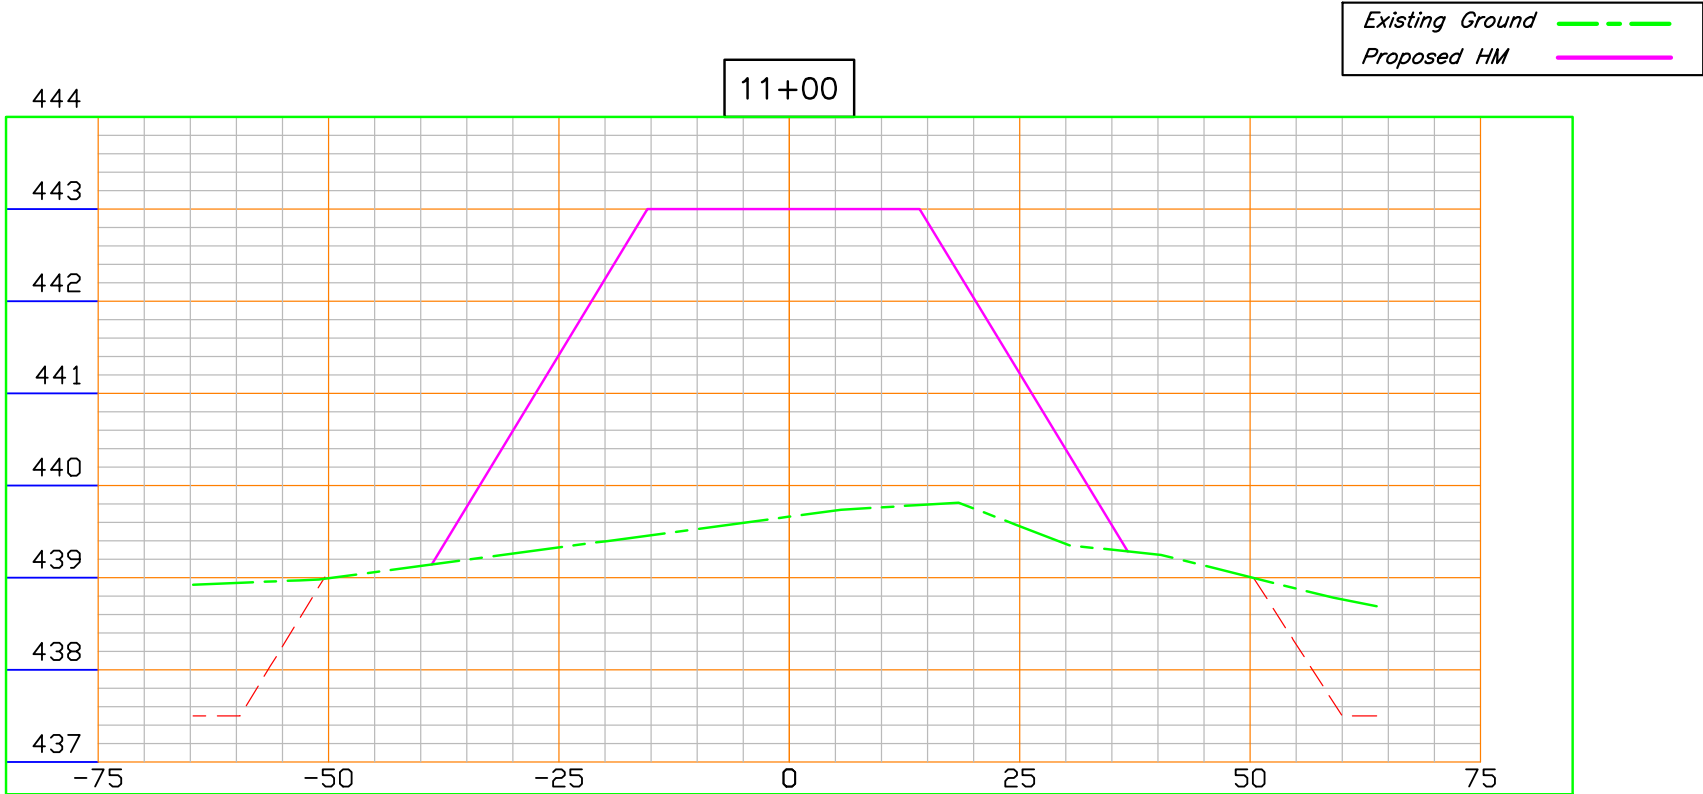

File No.	 United States Department of Agriculture Natural Resources Conservation Service	HM3A X-SECTIONS (1) Daugherty Wetland	Designed <u>Kerry Bushue</u> <u>10/23/23</u>
Drawing No.			Drawn <u>Kerry Bushue</u> <u>10/23/23</u>
Sheet <u>11</u> of <u>48</u>			Checked <u>M. Dasenbrock 8.2025</u> Approved <u>M. Dasenbrock 8.2025</u>
		York Twnshp, . Sec 27 T 9N R 11W Clark County County, IL.	

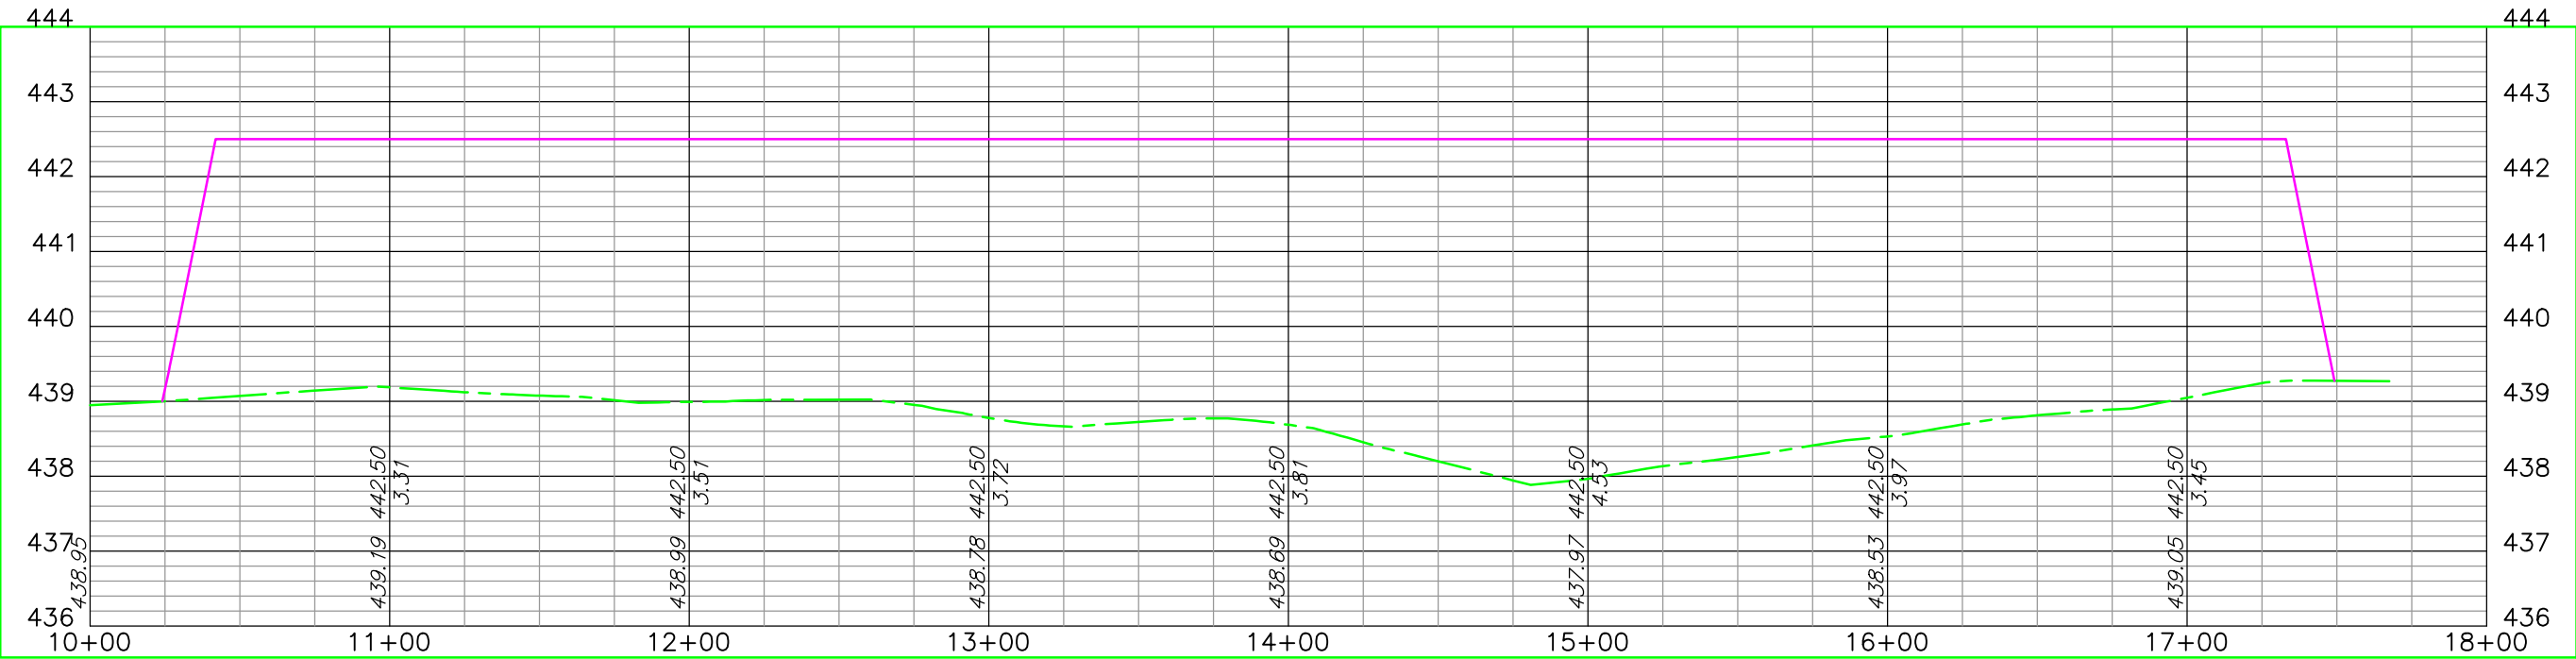

Existing Ground
Proposed HM




Designed Kerry Bushue 10/23/23
Drawn Kerry Bushue 10/23/23
Checked M. Daanbroeck 8/20/25
Approved M. Daanbroeck 8/20/25




HM4 PROFILE
Daugherty Wetland




File No. _____
Drawing No. _____
Sheet 4 of 4

York Twnshp, . Sec27 T 9N R 11W Clark County, IL.

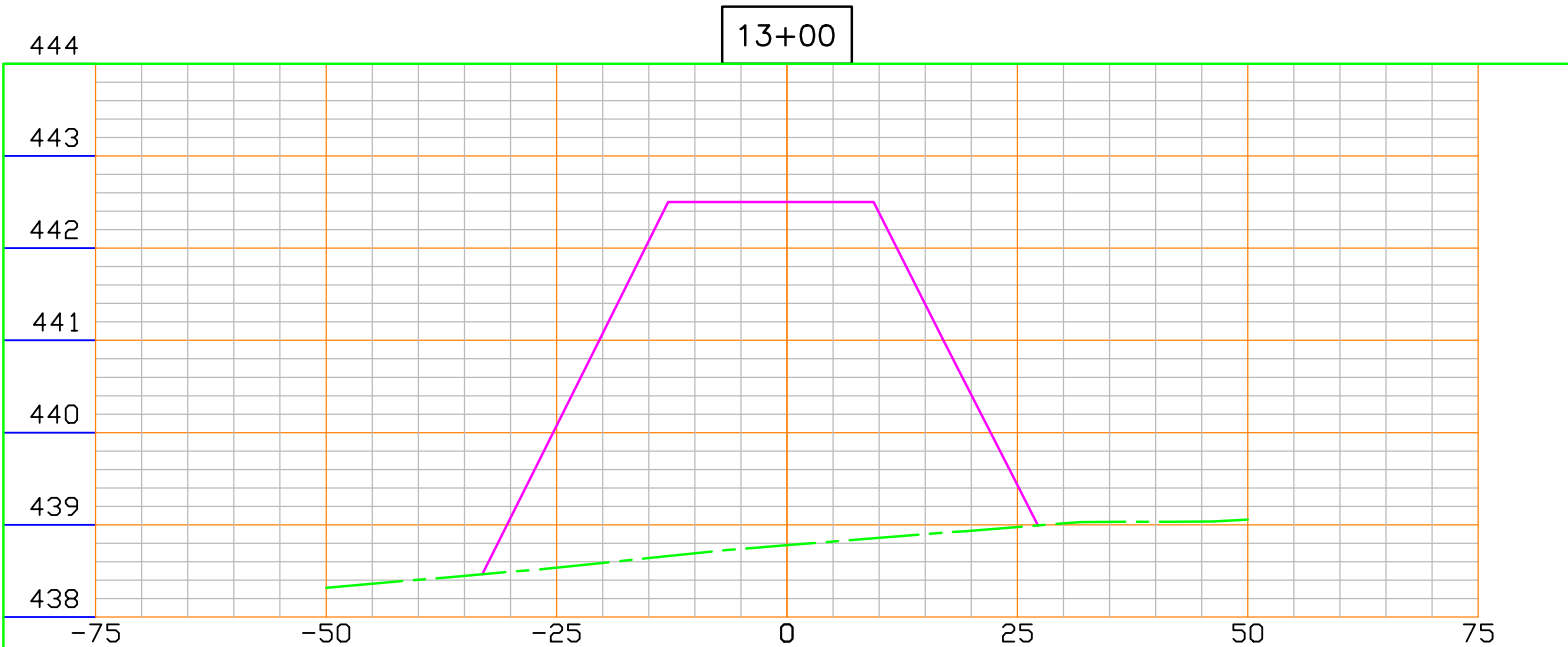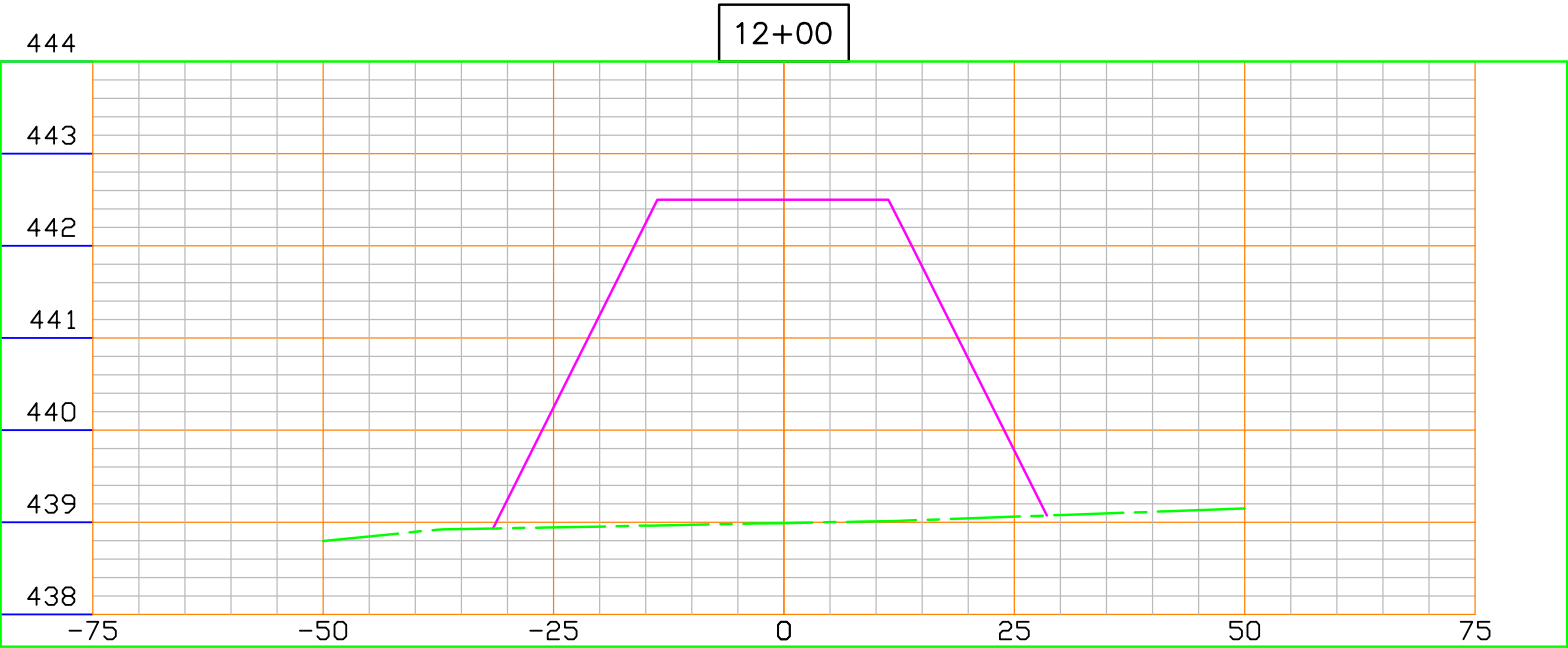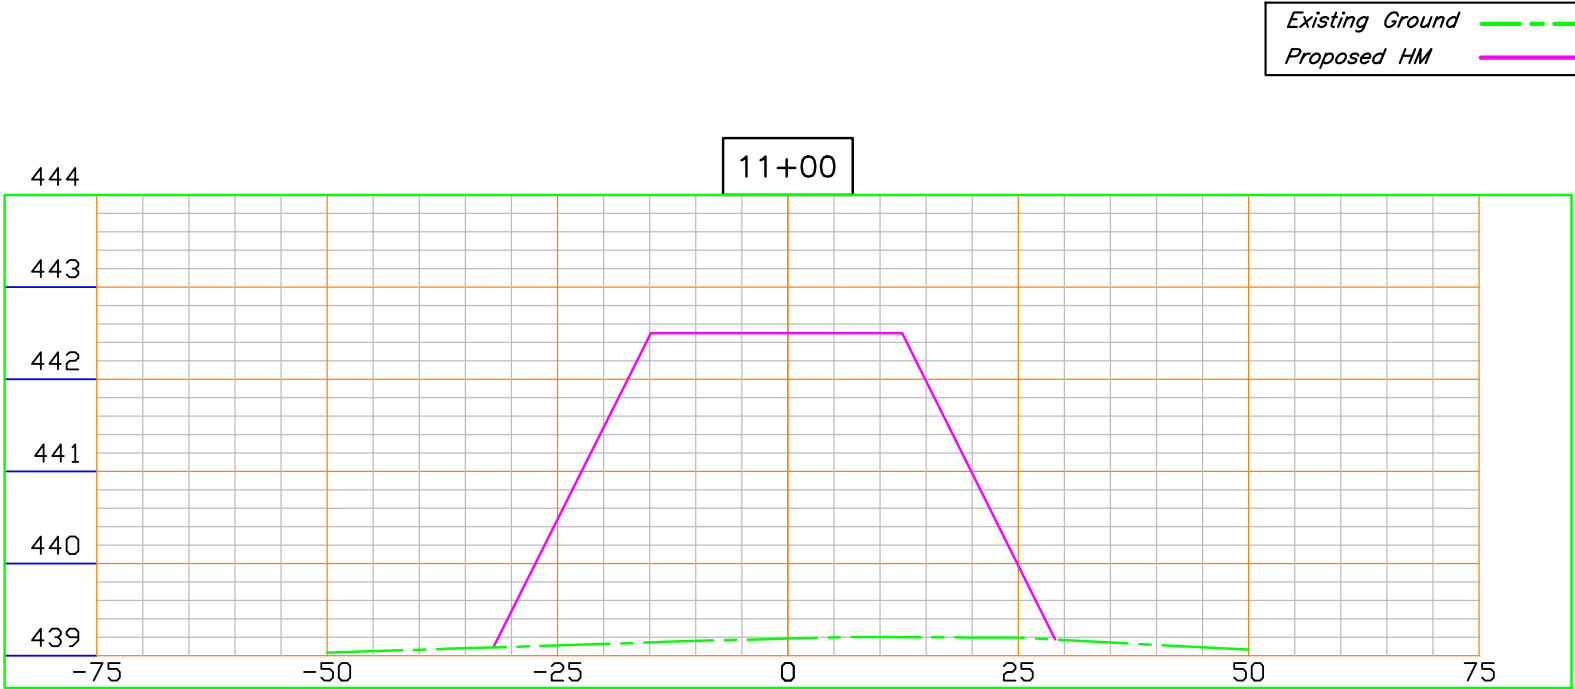

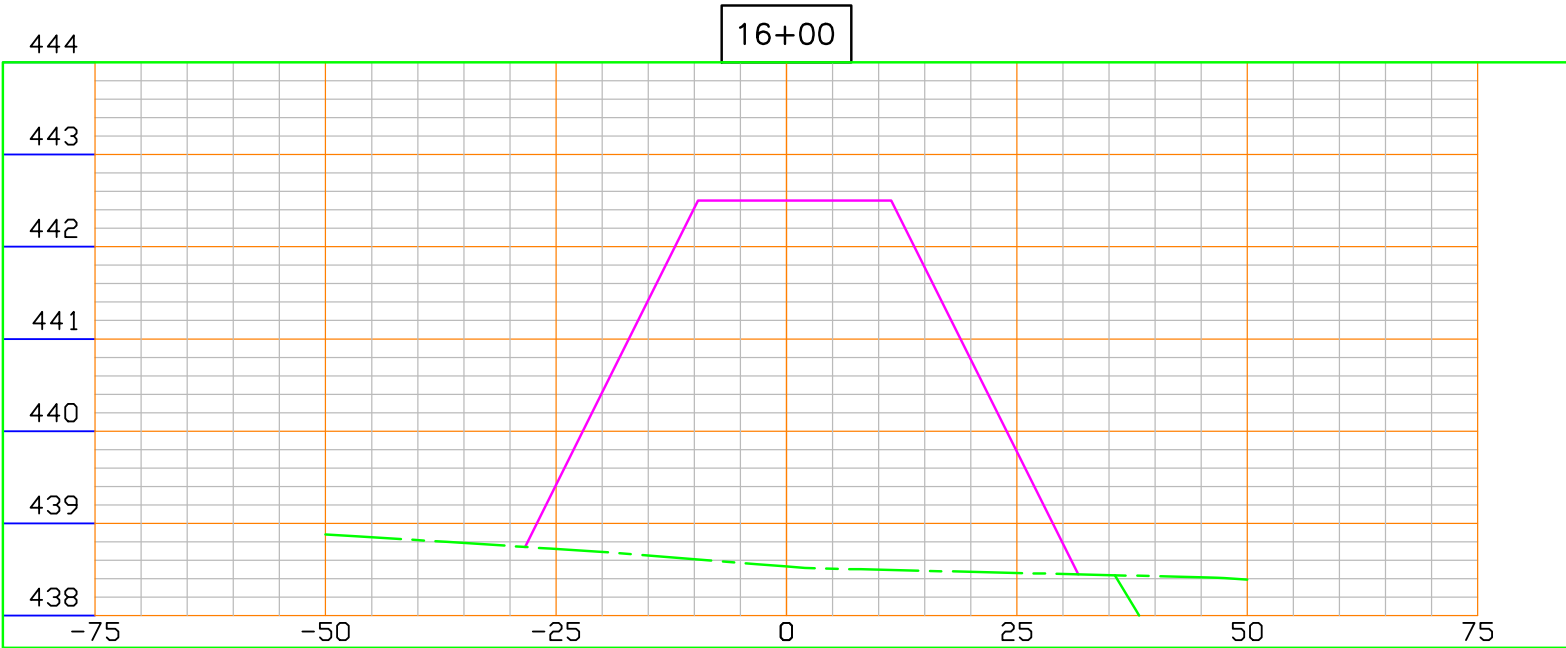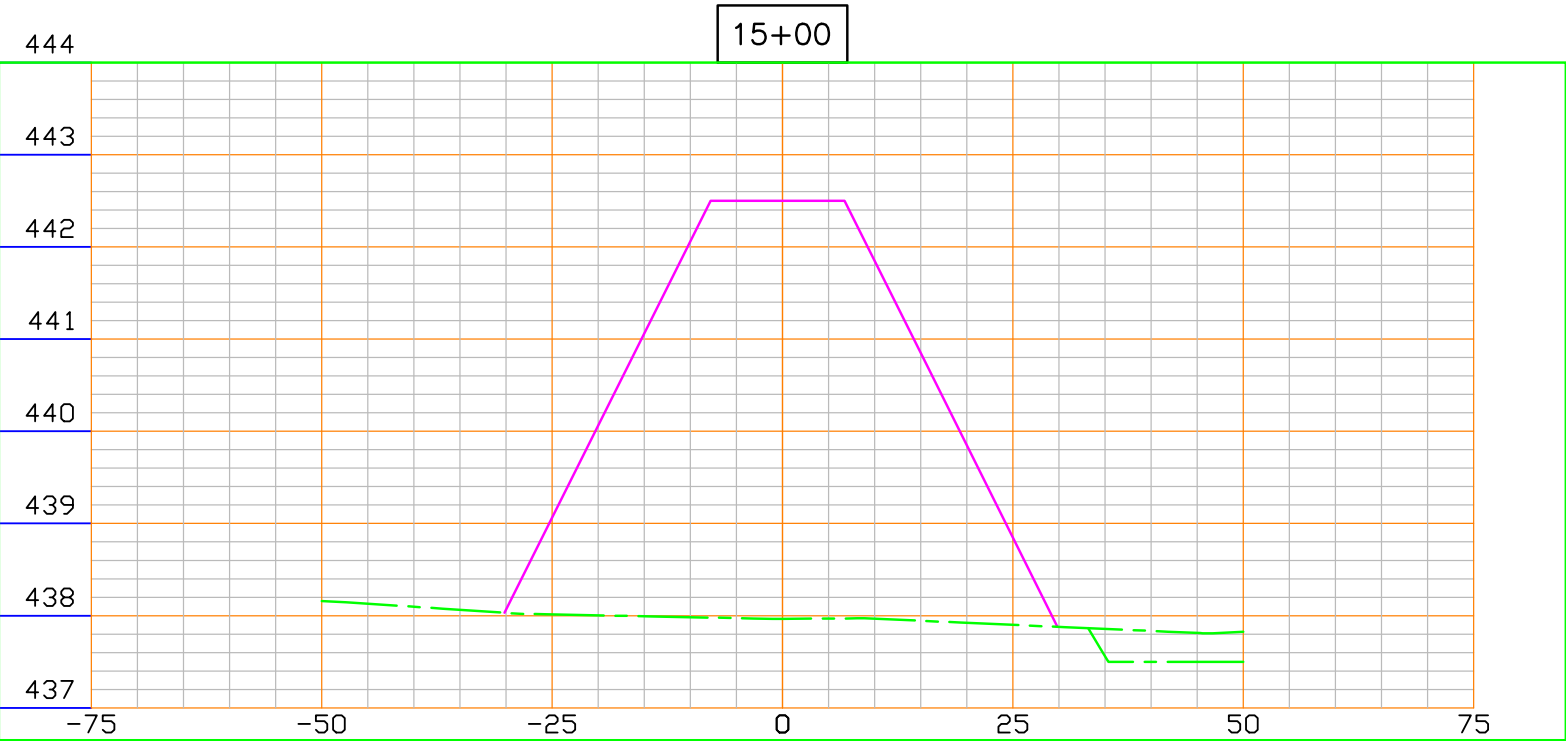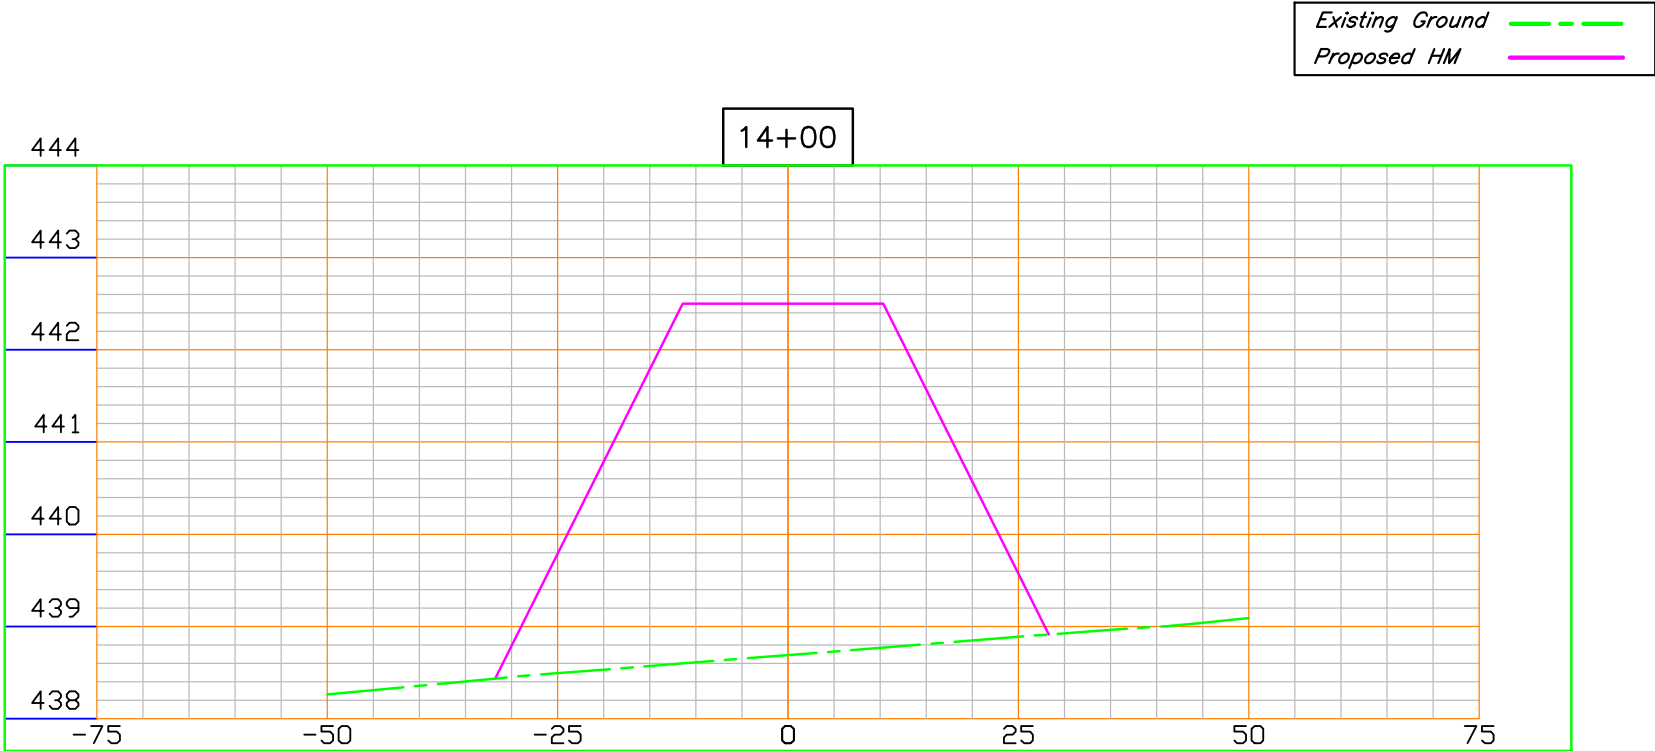

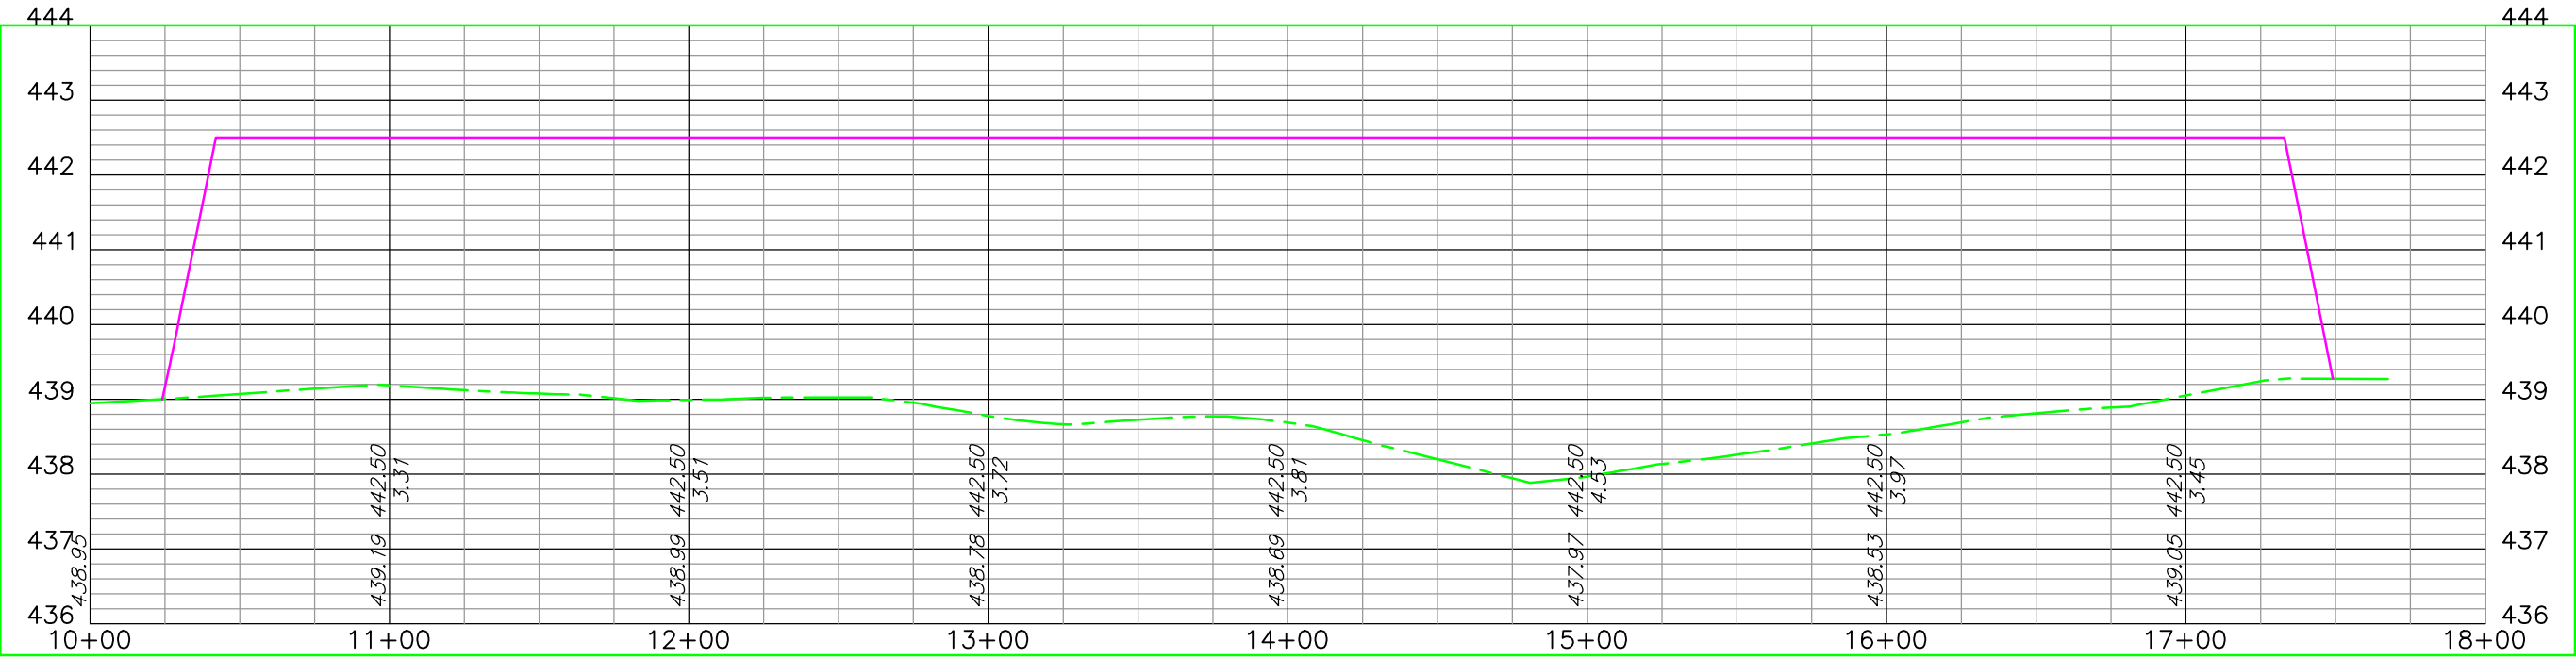




Designed	Kerry Bushue	Date	10/23/23
Drawn	Kerry Bushue	Date	10/23/23
Checked	M. Daenbroeck	Date	8.2025
Approved	M. Daenbroeck	Date	8.2025




York Twnshp, . Sec27 T 9N R 11W Clark County, IL.



HM5 PROFILE
Daugherty Wetland




File No.
Drawing No.
Sheet ### of ###

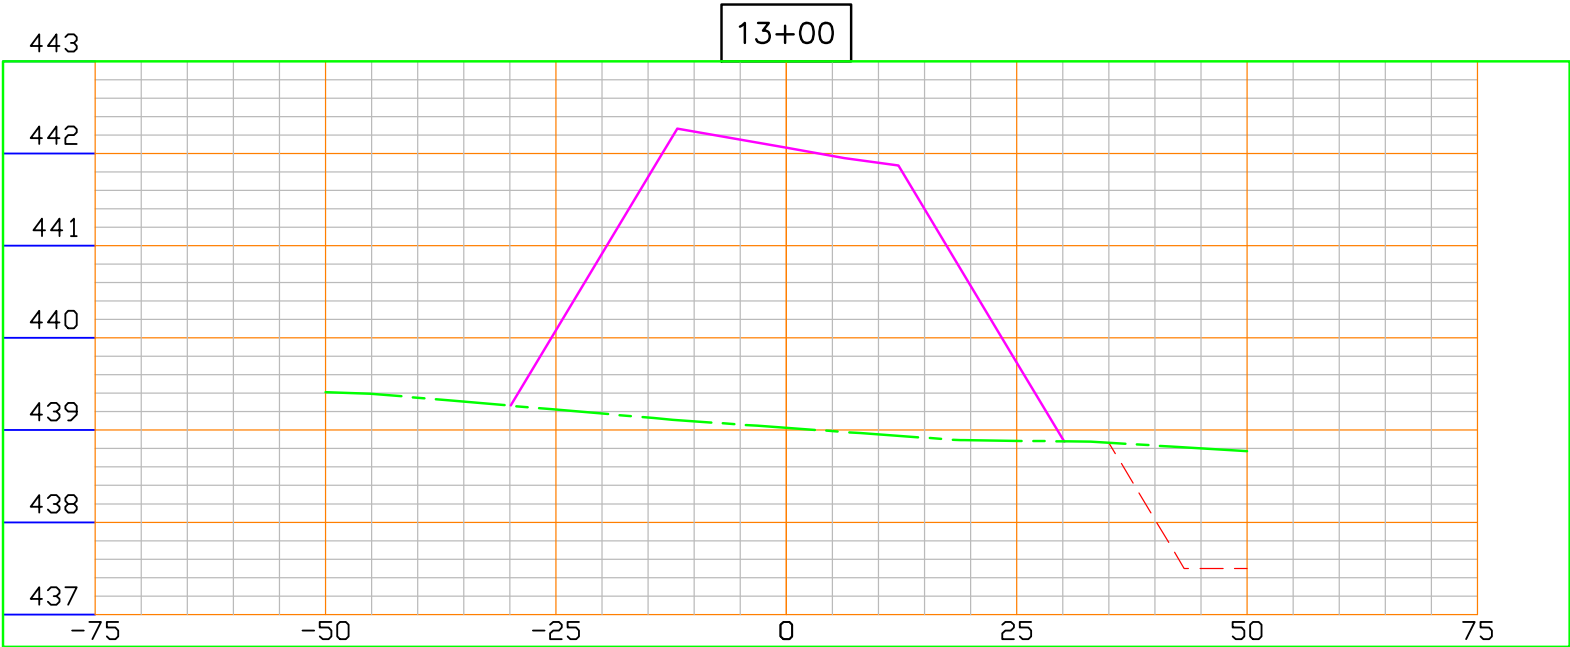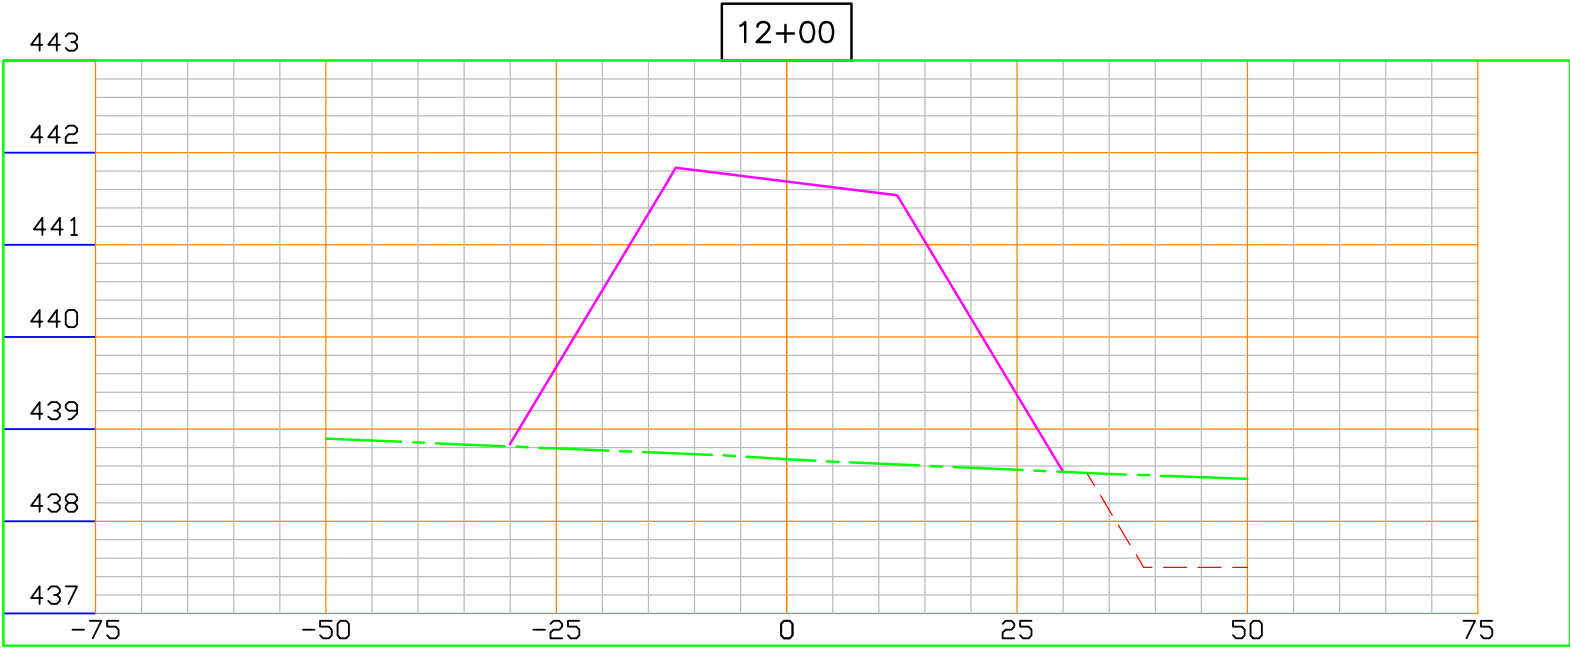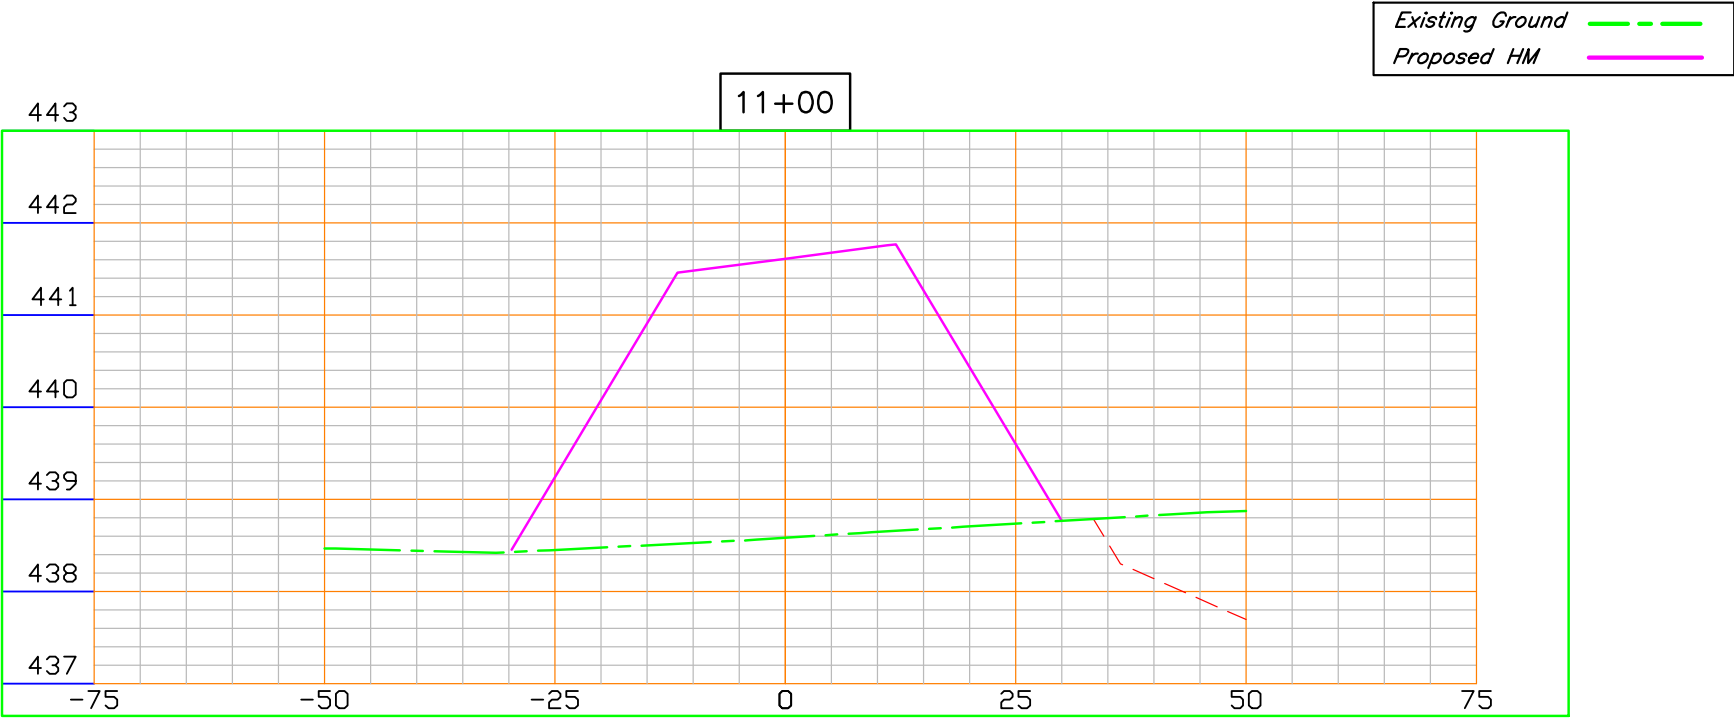

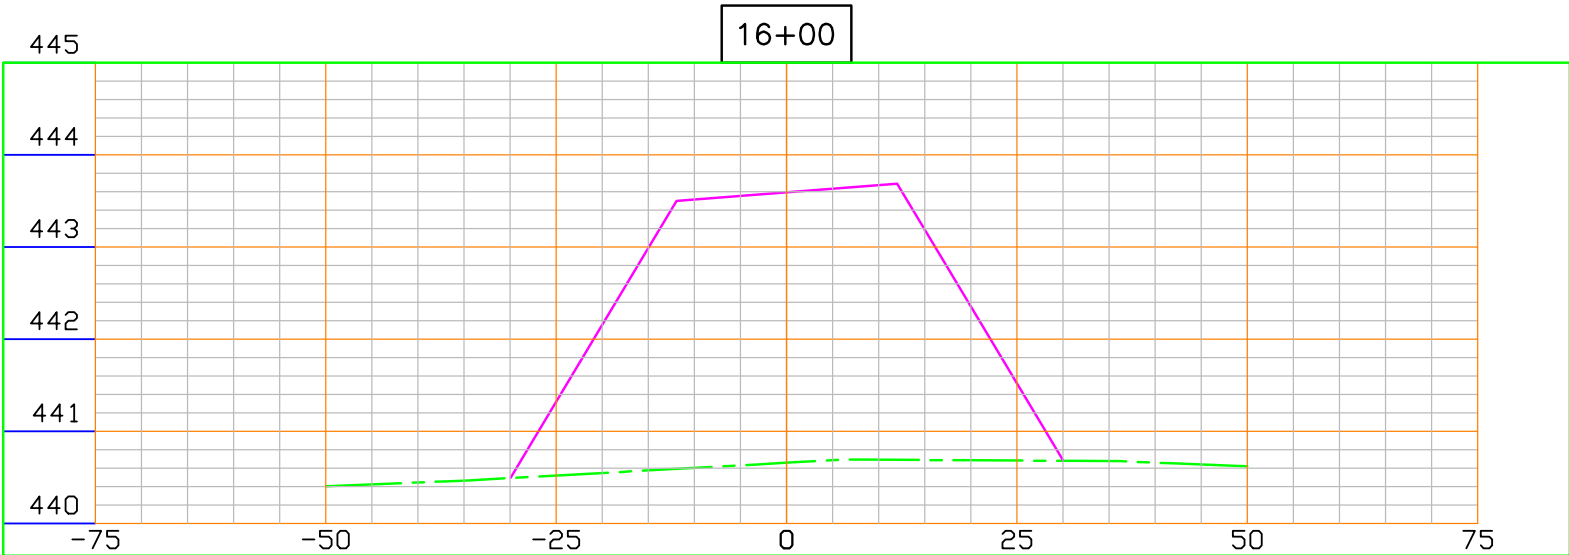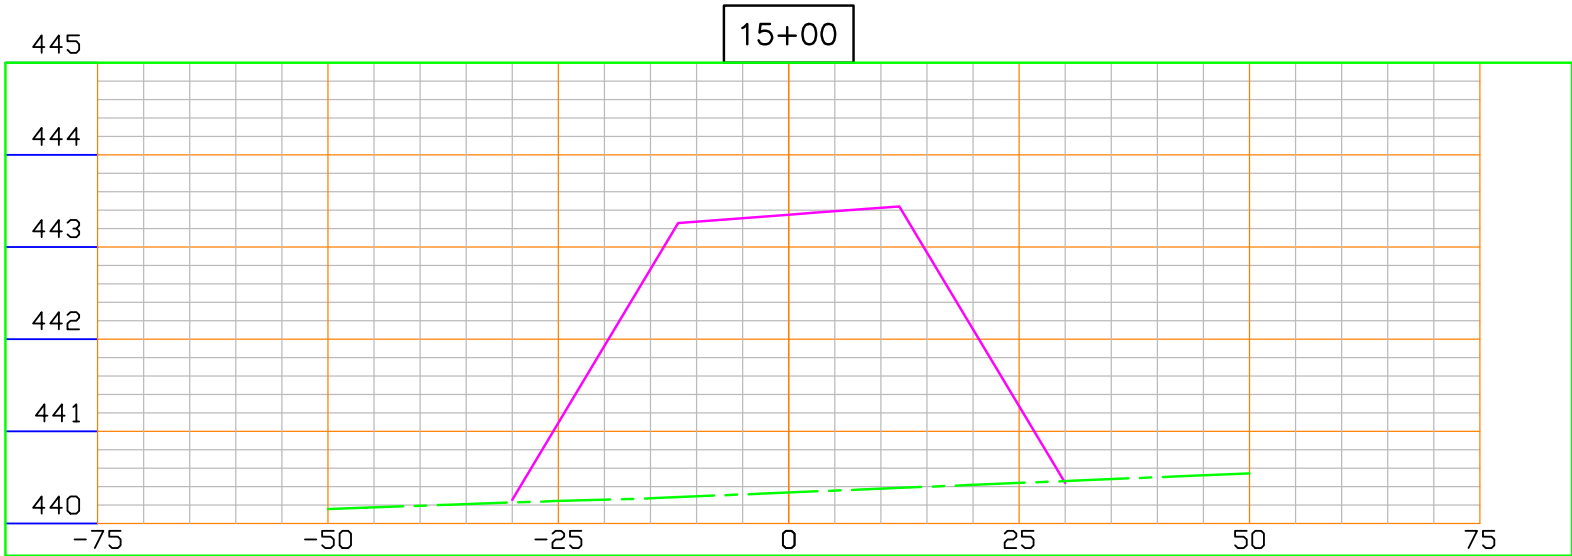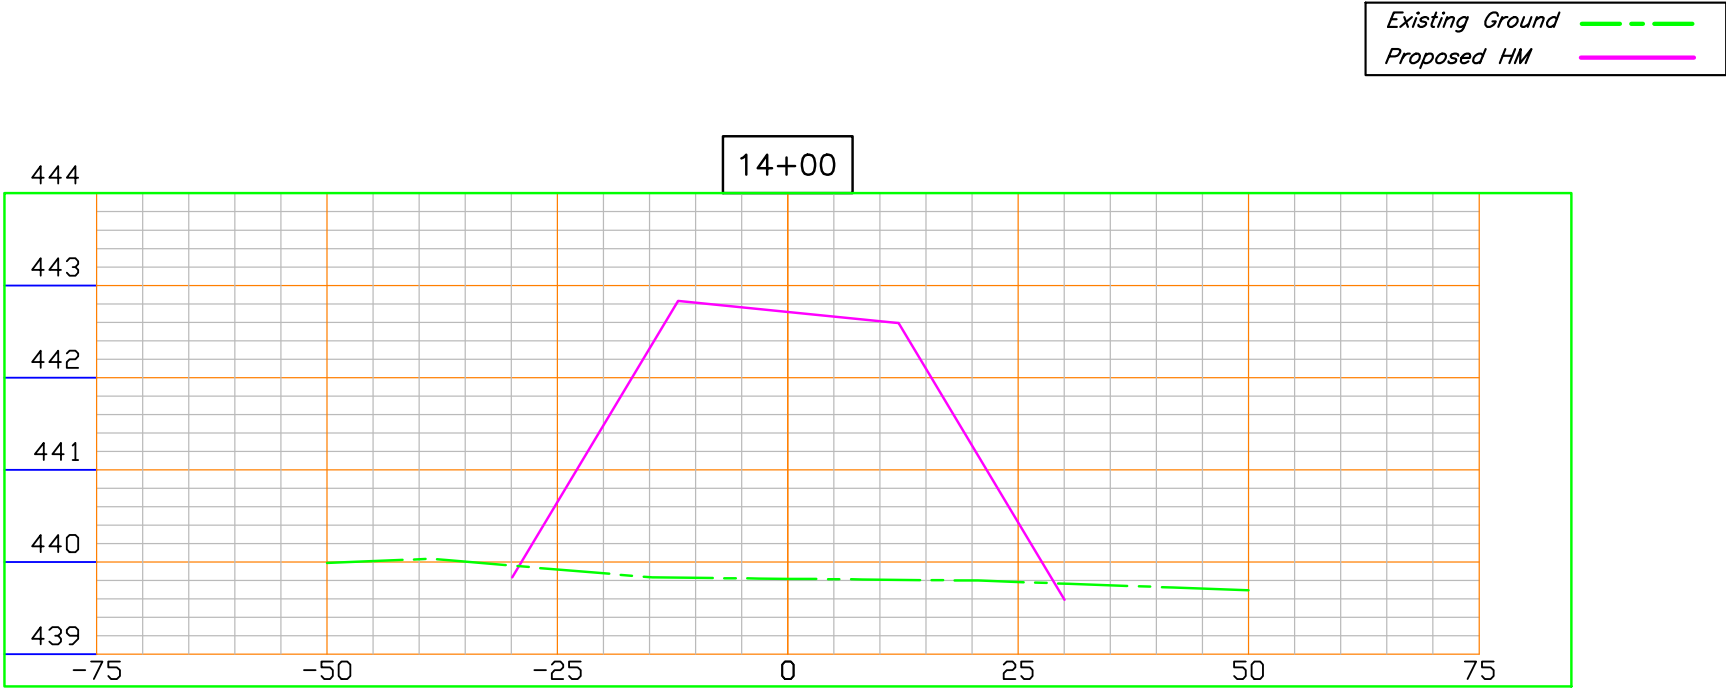

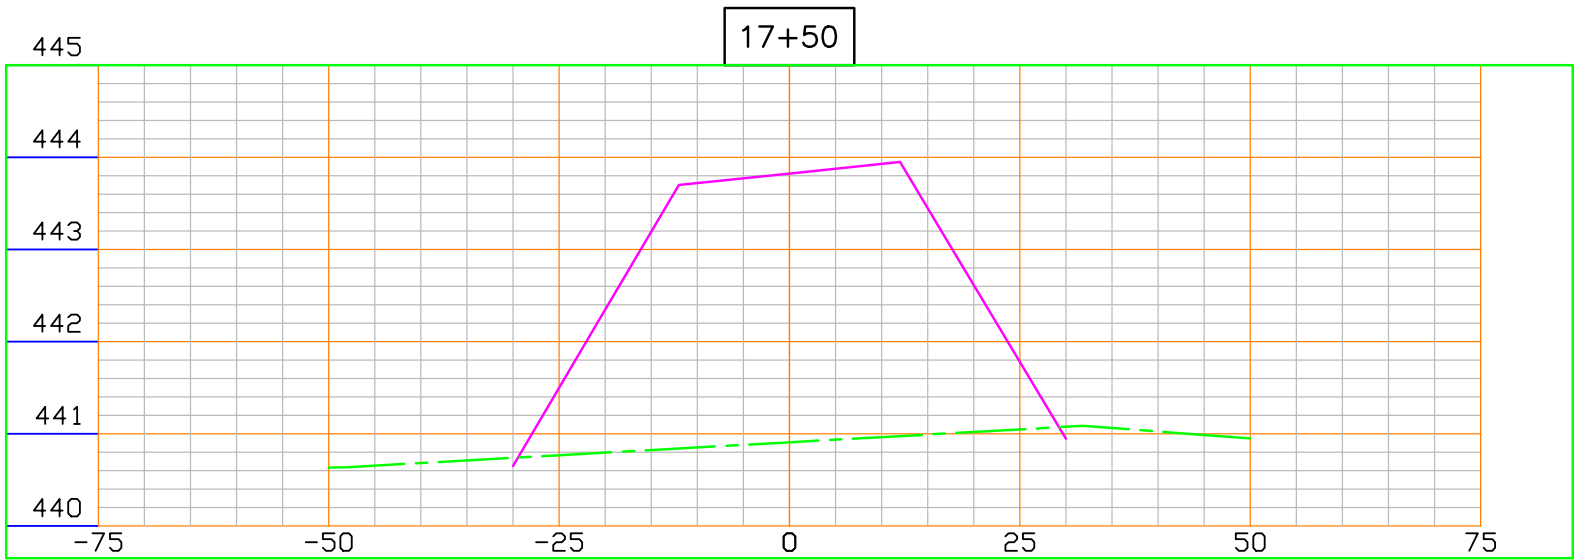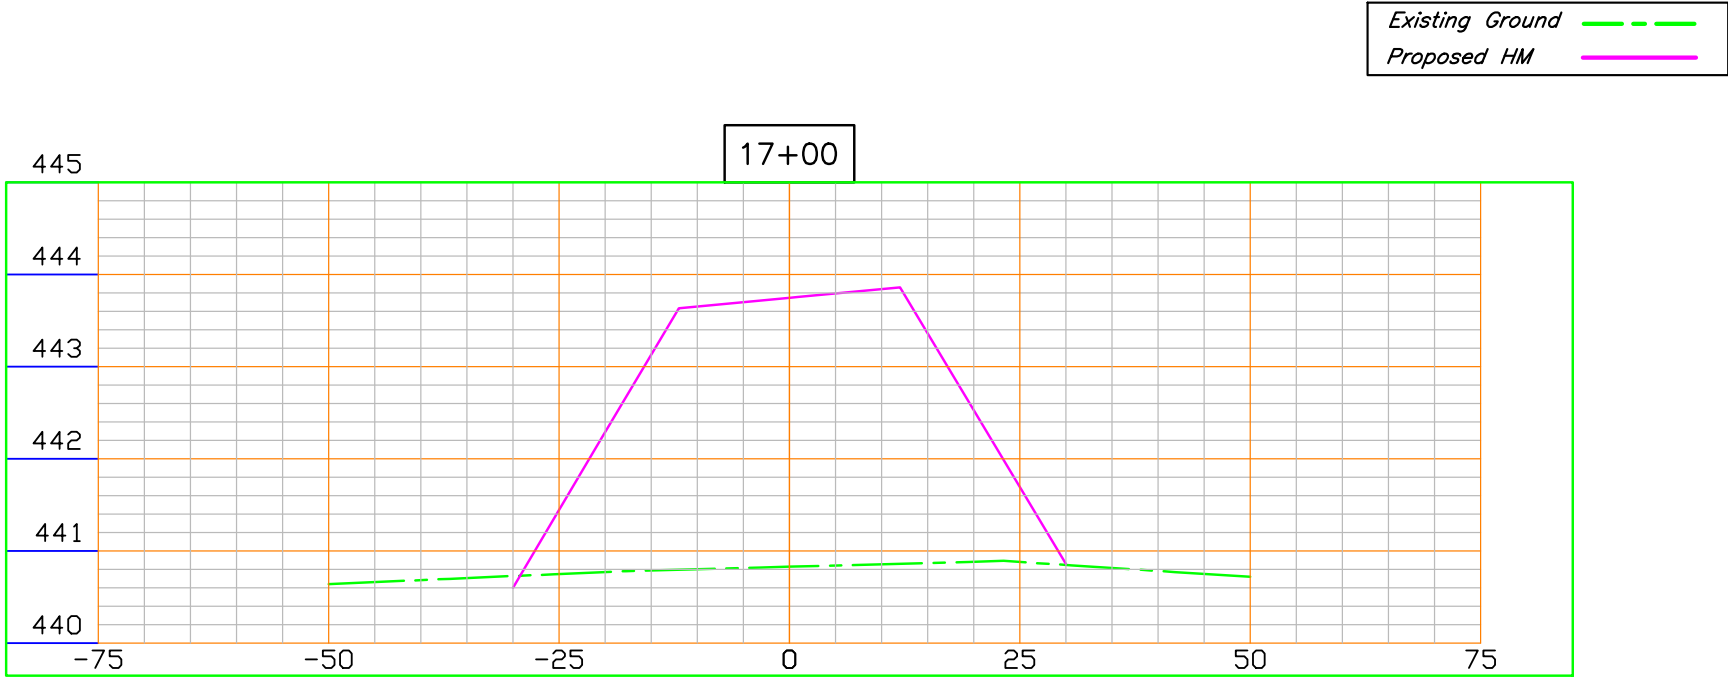

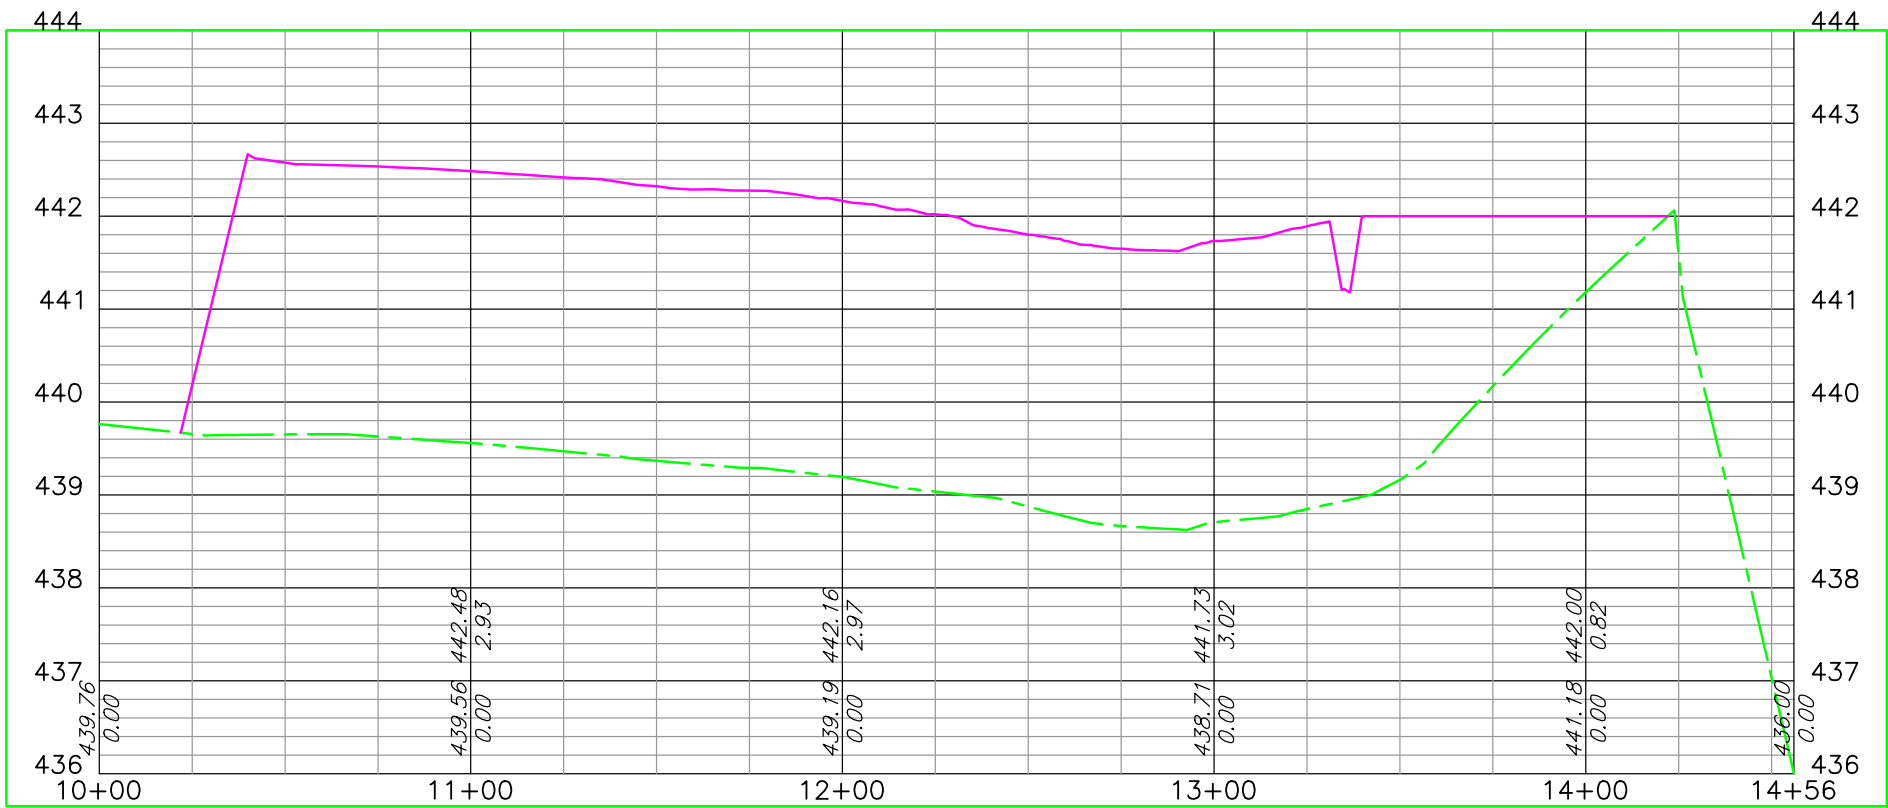




Existing Ground
Proposed HM

Designed Kerry Bushue 10/23/23
Drawn Kerry Bushue 10/23/23
Checked M. Daenbrock 8/20/25
Approved M. Daenbrock 8/20/25


HM6 PROFILE
Daugherty Wetland
York Twnshp., Sec27 T9N R11W Clark County, IL.



File No.
Drawing No.
Sheet 4 of 7

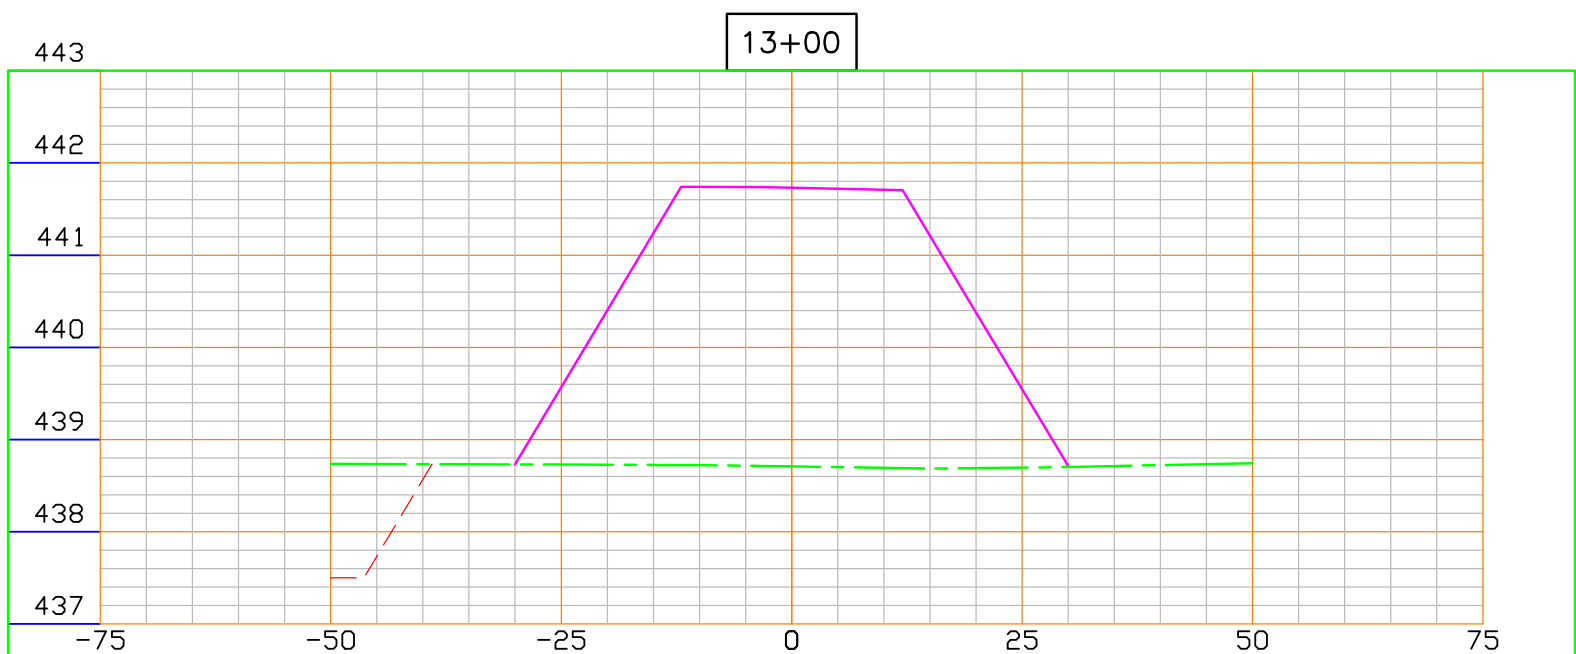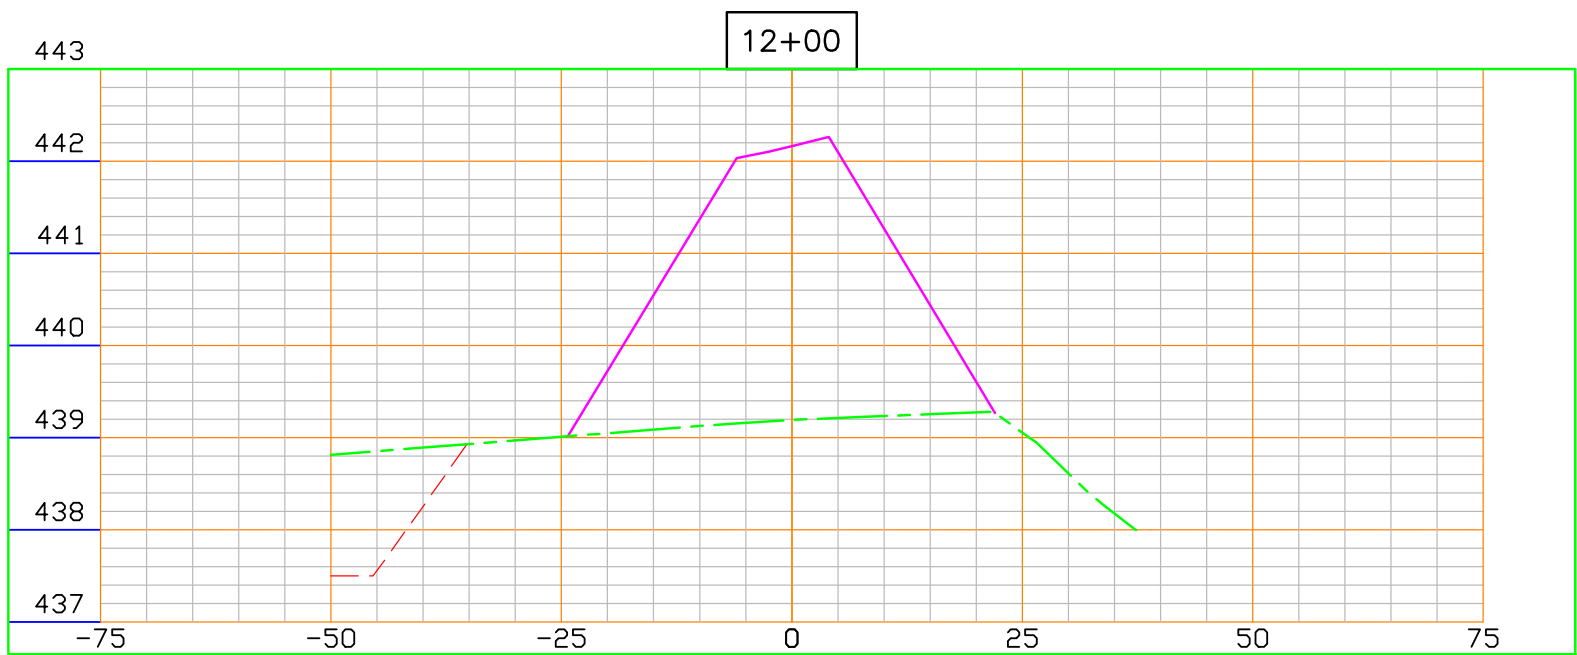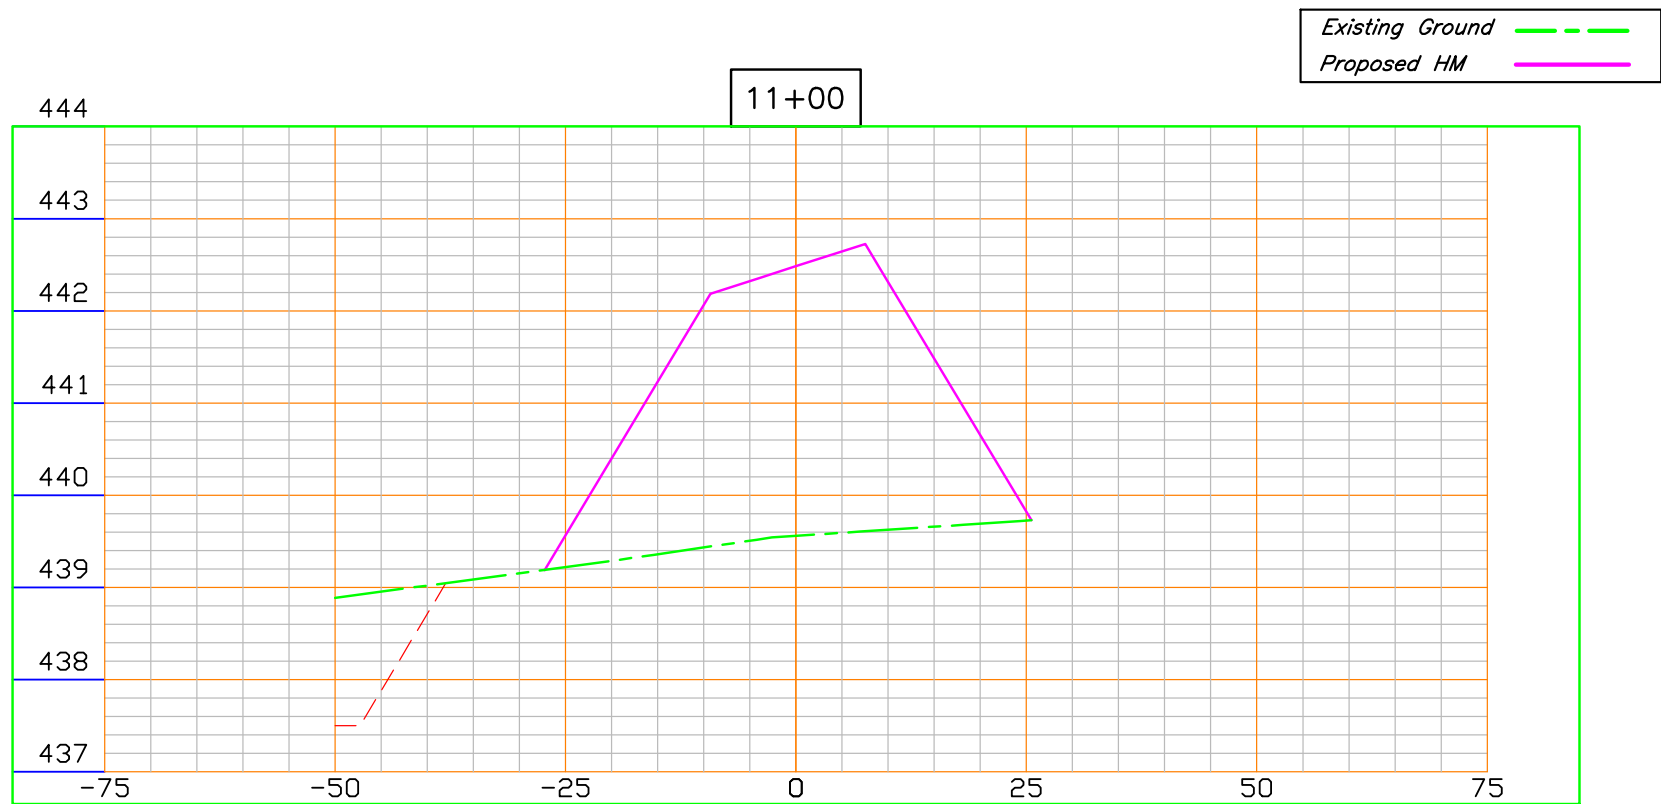

File No.	 United States Department of Agriculture Natural Resources Conservation Service	HM6 X-SECTIONS (1) Daugherty Wetland	Designed <u>Kerry Bushue</u> <u>10/23/23</u>	
Drawing No.			Drawn <u>Kerry Bushue</u> <u>10/23/23</u>	
Sheet <u>0000</u> of <u>0000</u>			Checked <u>M. Dasenbrock</u> <u>8.2025</u>	
York Twnshp, .		Sec 27 T 9N R 11W	Clark County County, IL.	Approved <u>M. Dasenbrock</u> <u>8.2025</u>

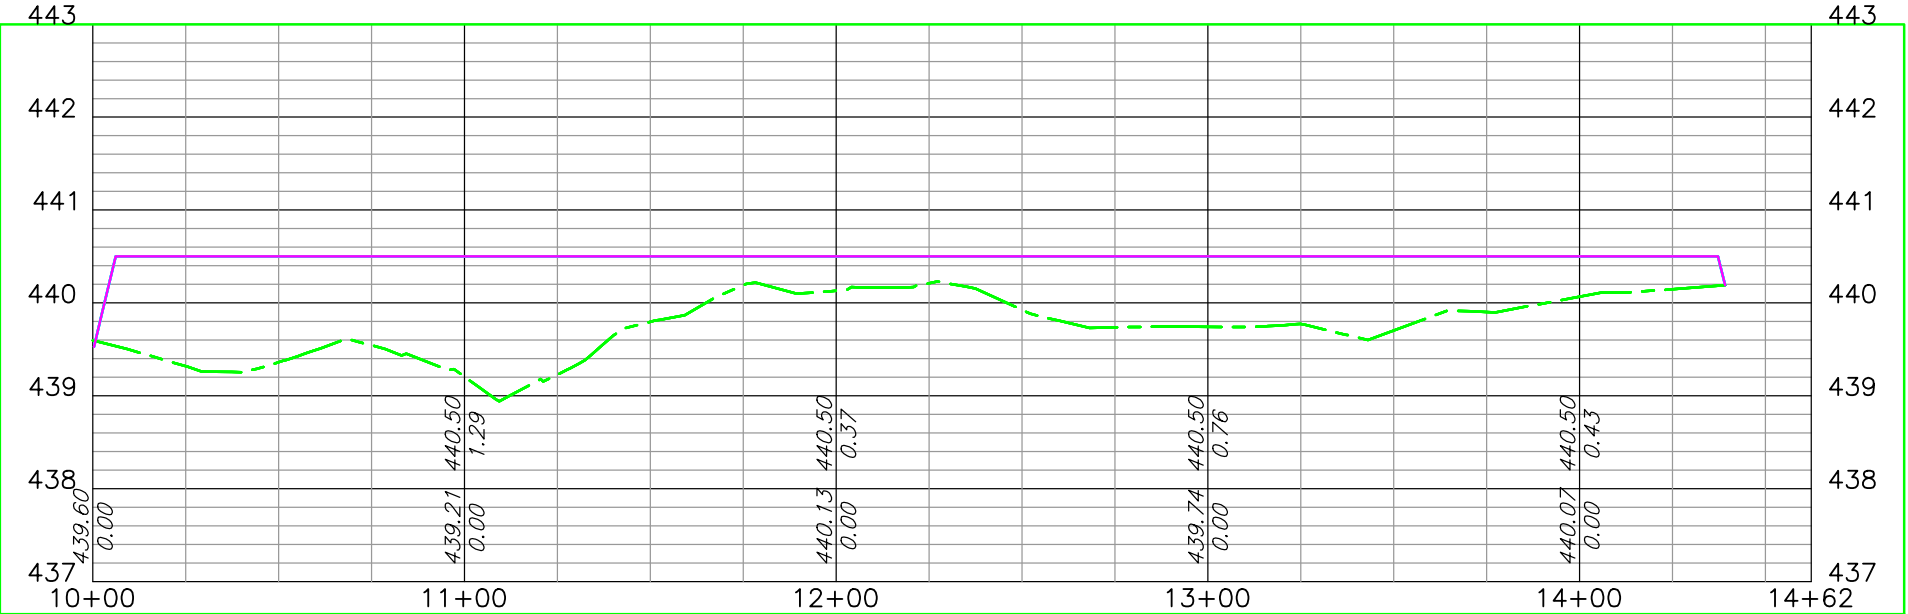





Existing Ground
Proposed HM

Designed: Kerry Bushue 10/23/23
Drawn: Kerry Bushue 10/23/23
Checked: M. Dasenbrock 8.2025
Approved: M. Dasenbrock 8.2025


HM7 PROFILE
Daugherty Wetland
York Twnshp., Sec 27 T 9N R 11W Clark County, IL.



File No.
Drawing No.
Sheet 4 of 7

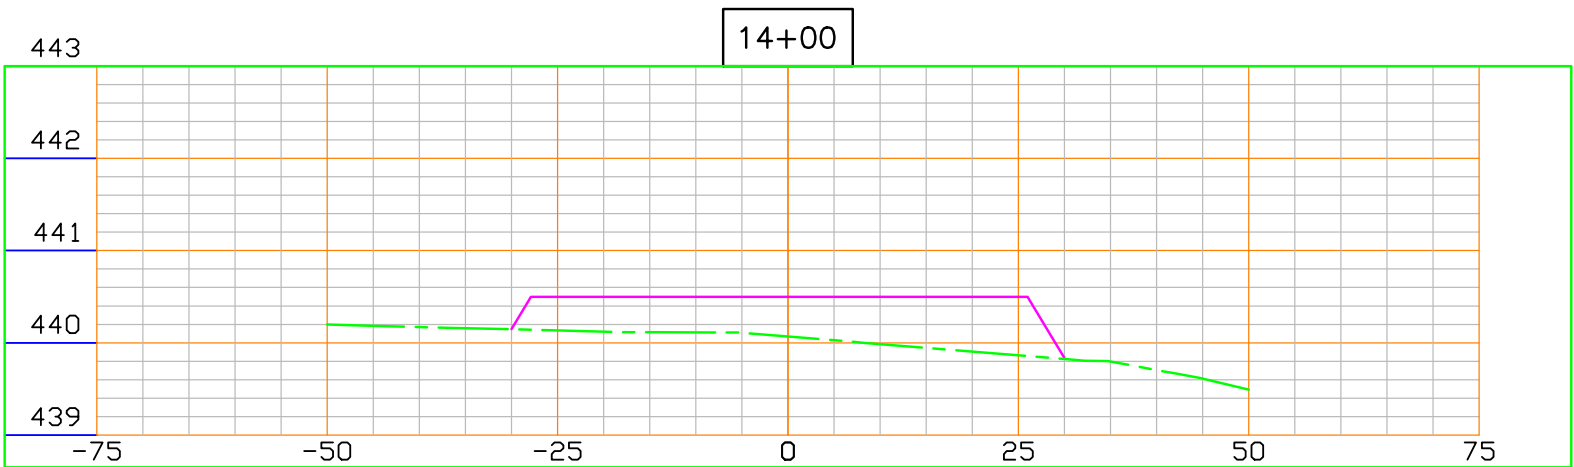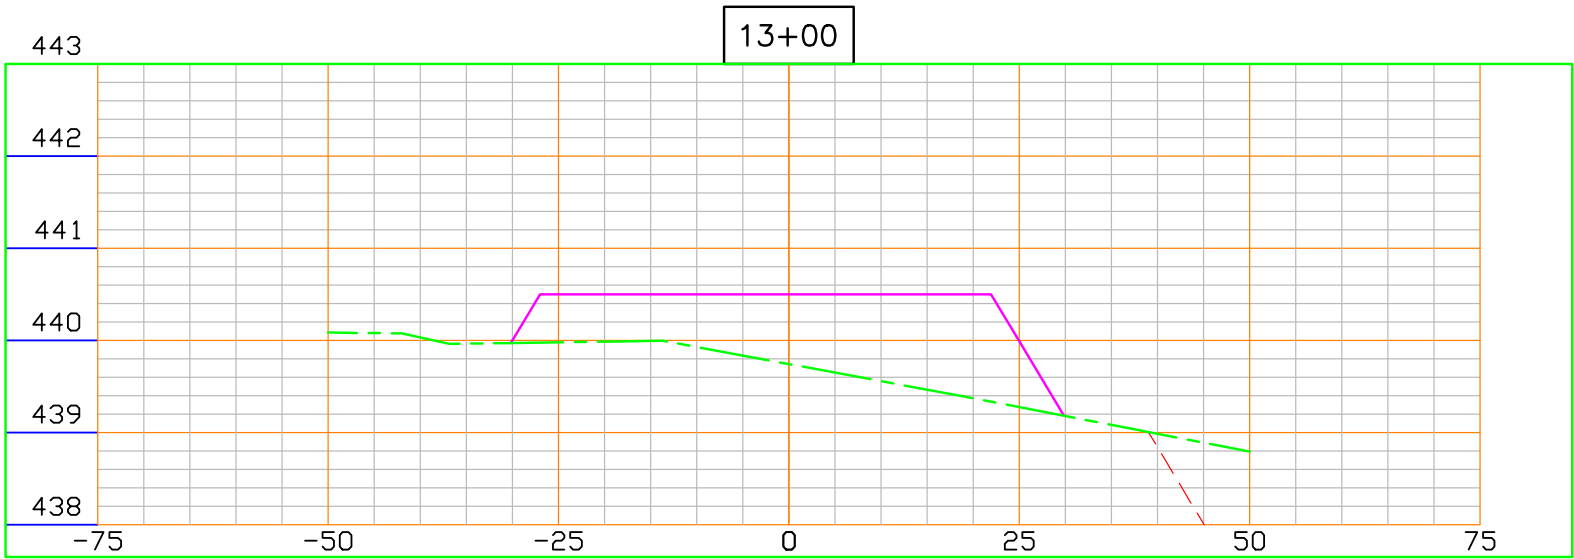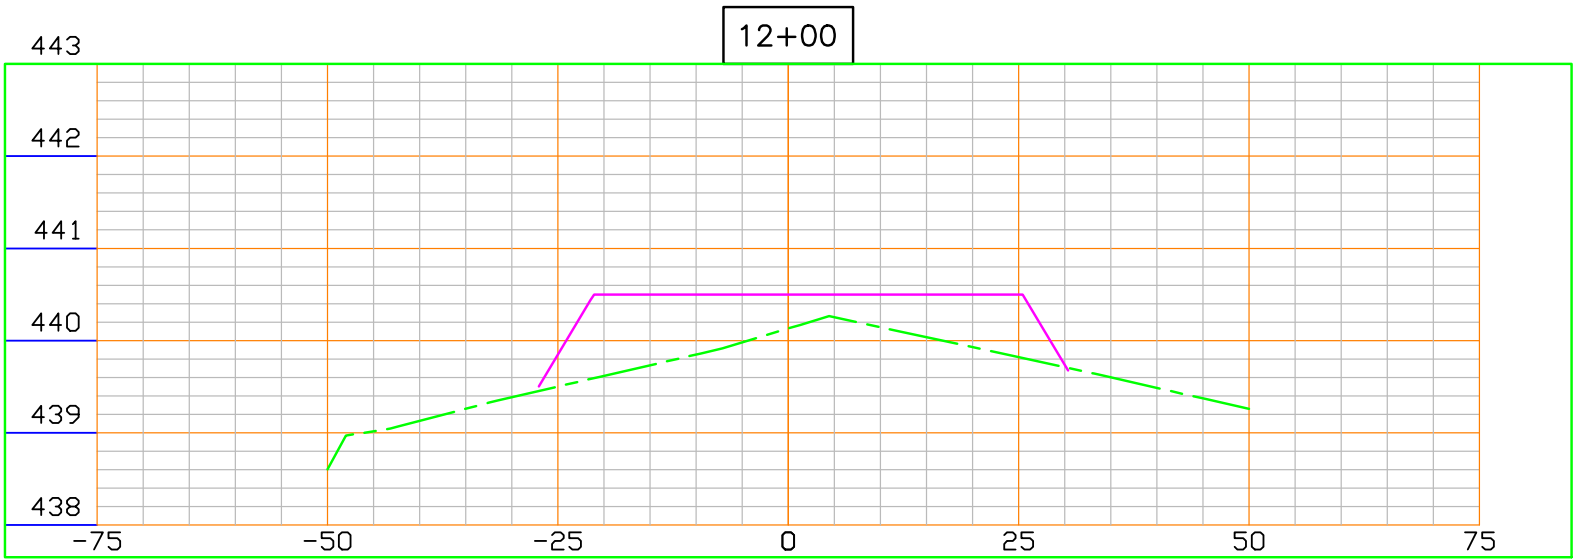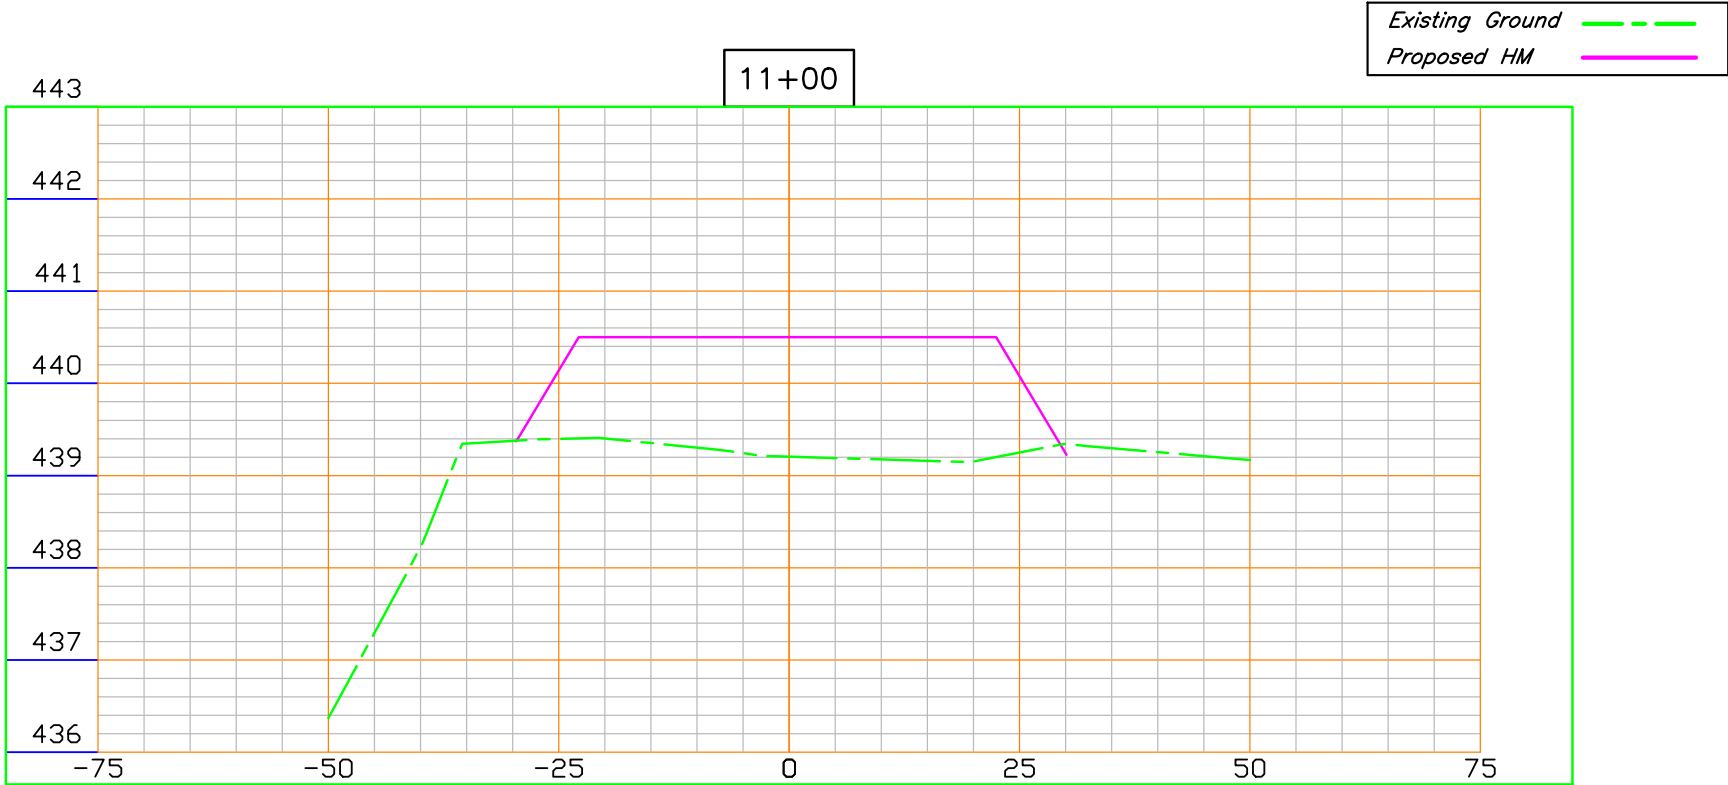

File No.	 United States Department of Agriculture Natural Resources Conservation Service	HM7 X-SECTIONS (1) Daugherty Wetland	Designed <u>Kerry Bushue</u> <u>10/23/23</u>
Drawing No.			Drawn <u>Kerry Bushue</u> <u>10/23/23</u>
Sheet <u>###</u> of <u>###</u>			Checked <u>M. Dasenbrock</u> <u>8.2025</u>
			Approved <u>M. Dasenbrock</u> <u>8.2025</u>
		York Twnshp, . Sec 27 T 9 N R 11 W Clark County County, IL.	

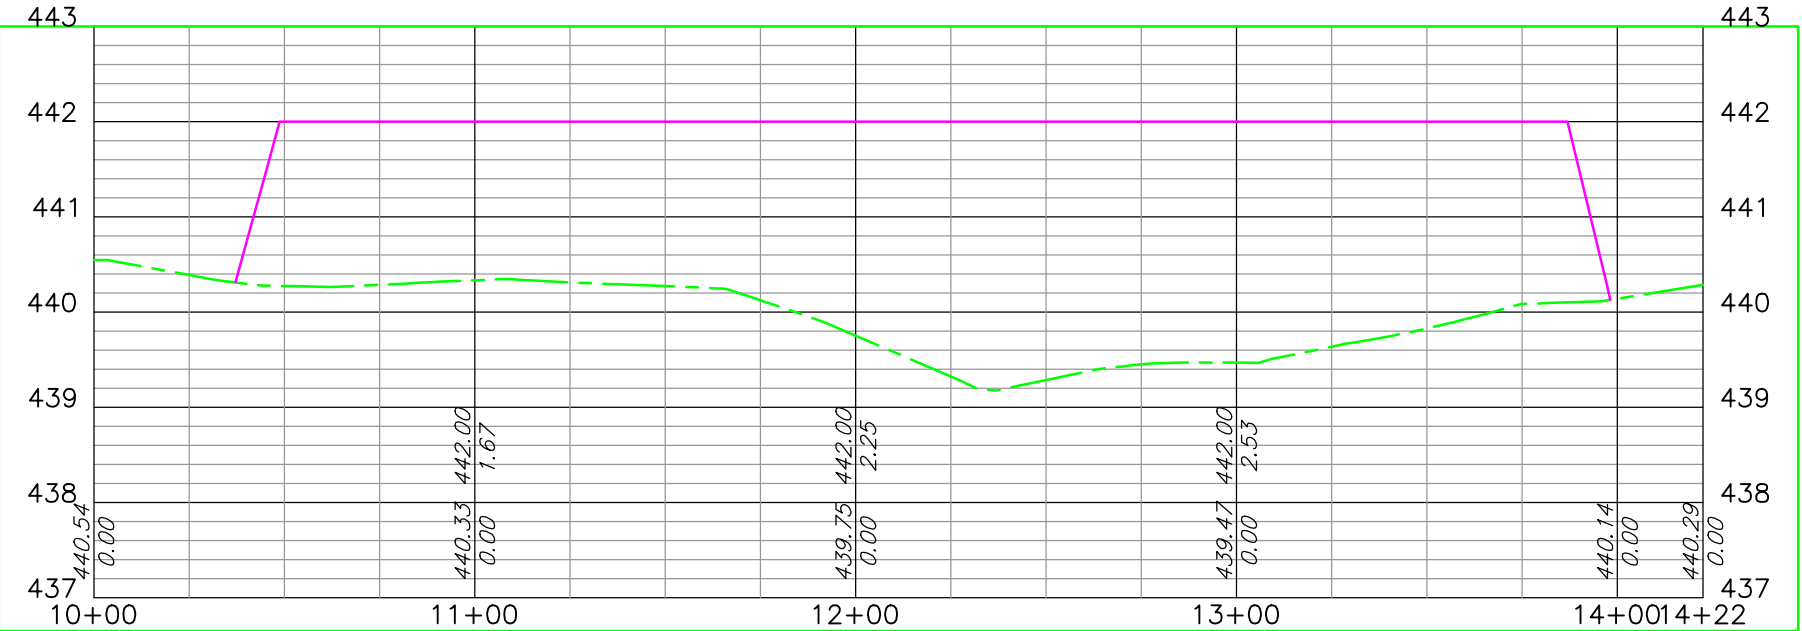




Existing Ground
Proposed HM


Designed Kerry Bushue 10/23/23
Drawn Kerry Bushue 10/23/23
Checked M. Daenbrock 8/20/25
Approved M. Daenbrock 8/20/25

HM8 PROFILE
Daugherty Wetland
York Twnshp, . Sec27 T 9N R 11W Clark County, IL.



File No. _____
Drawing No. _____
Sheet 4 of 4

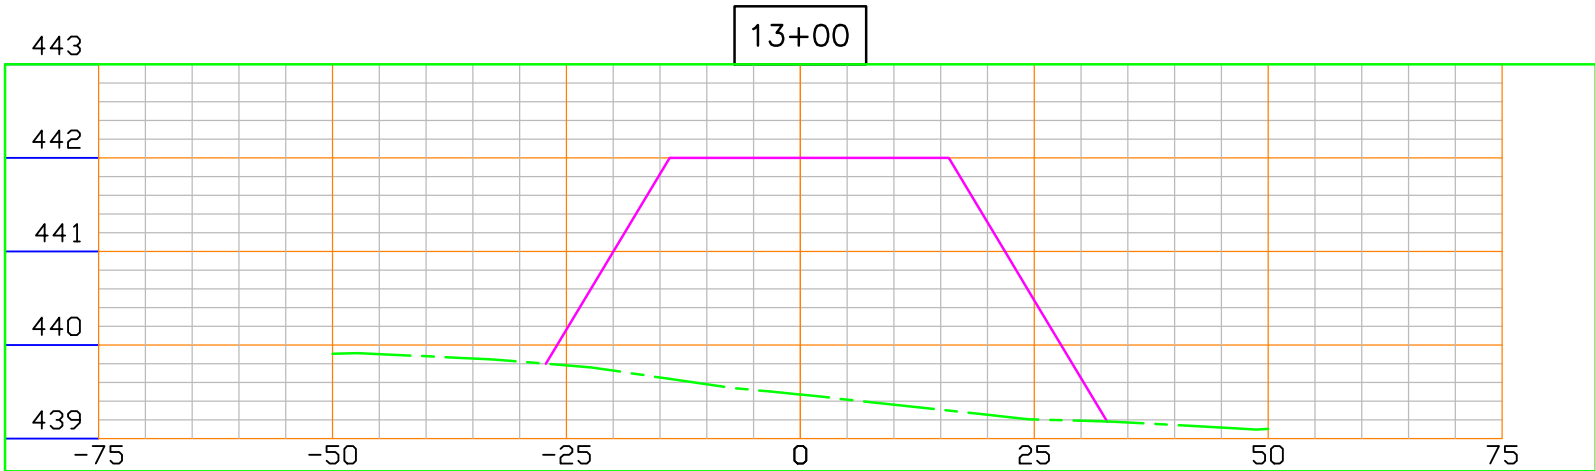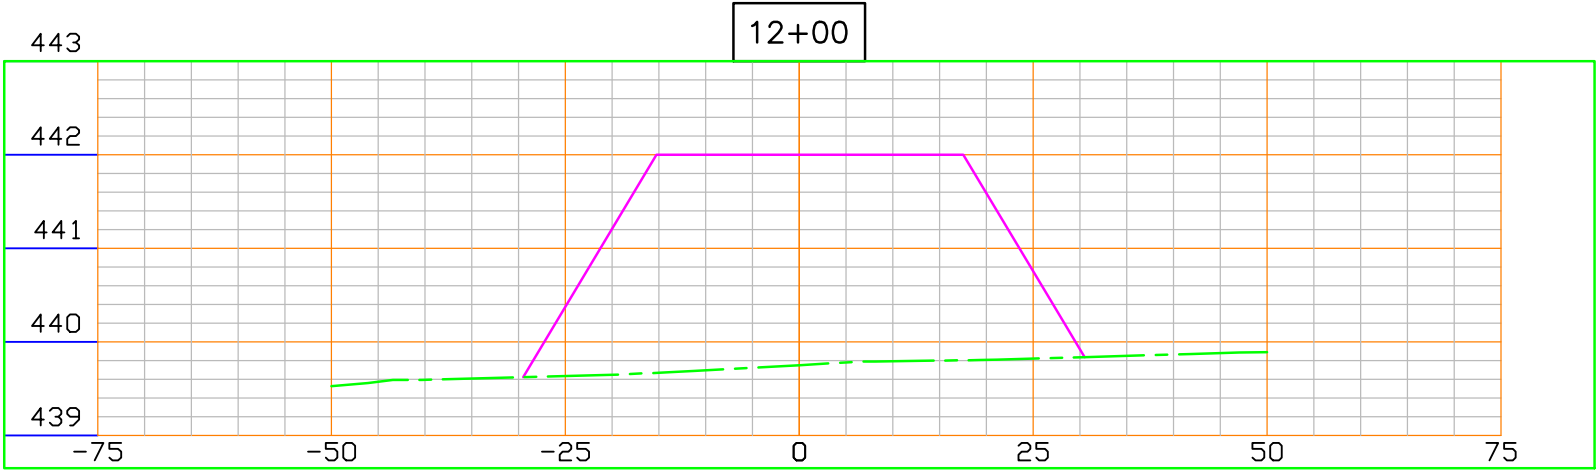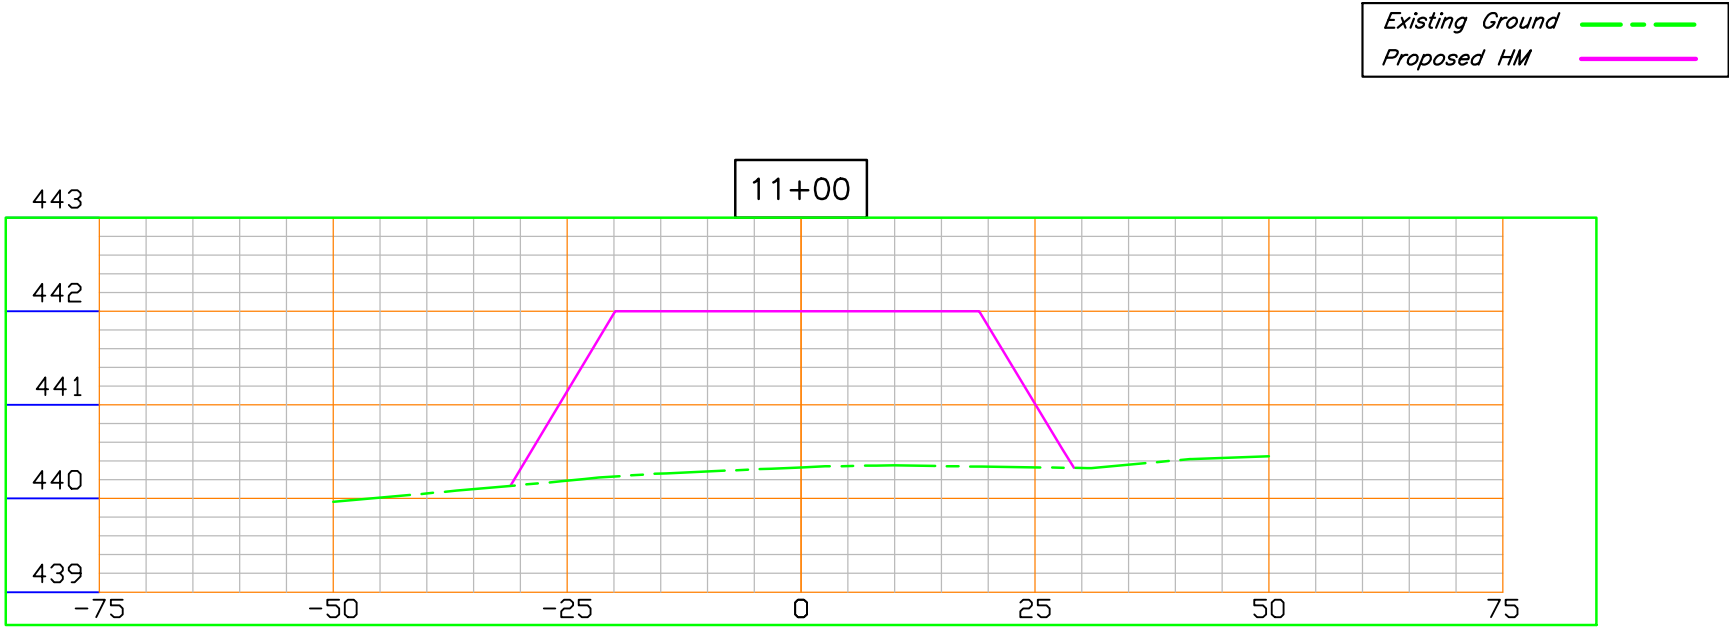

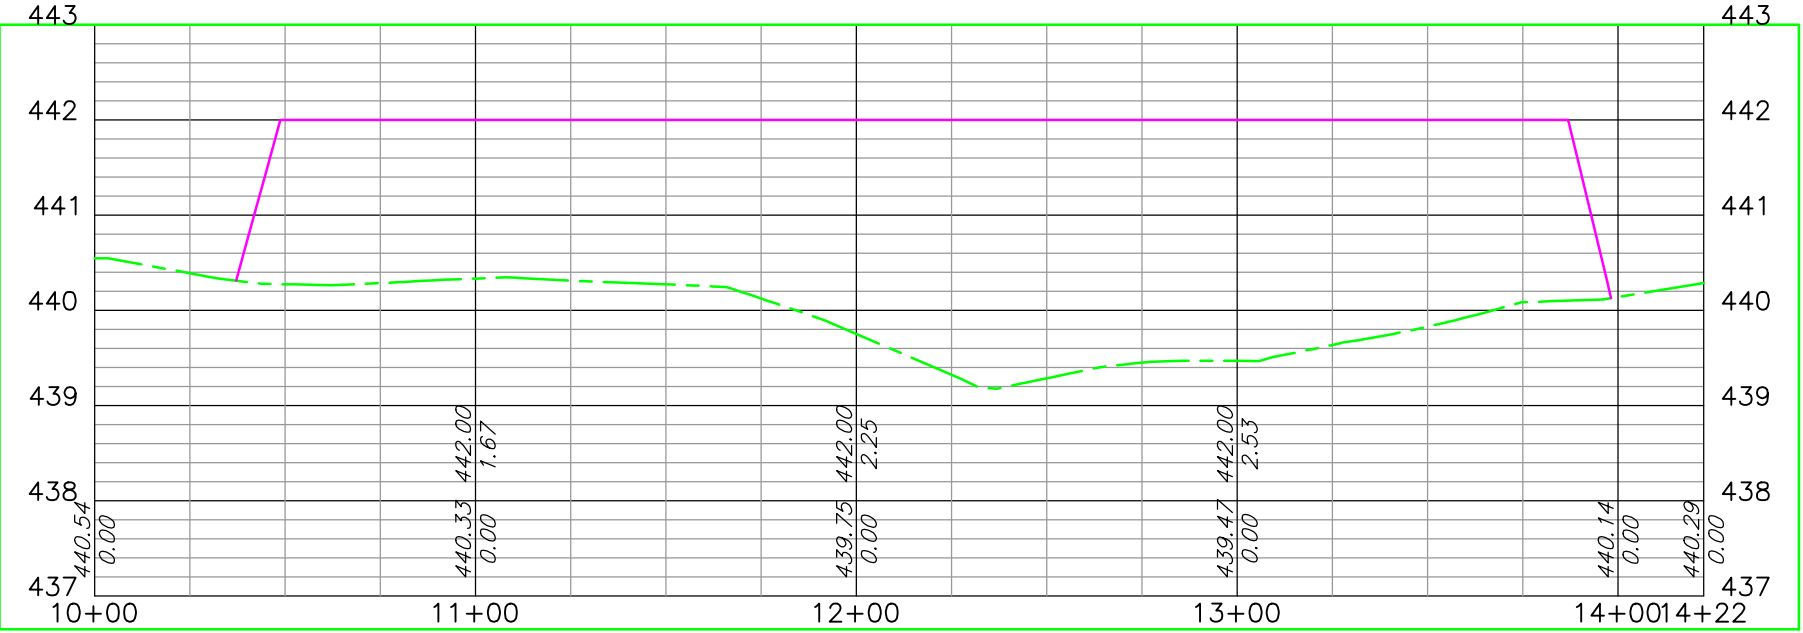

Existing Ground
Proposed HM





Designed Kerry Bushue 10/23/23
Drawn Kerry Bushue 10/23/23
Checked M. Dassenbrock 8.2025
Approved M. Dassenbrock 8.2025

York Twnshp, . Sec27 T 9N R 11W Clark County, IL.


United States
Department of
Agriculture
USDA
Natural Resources
Conservation Service

File No.
Drawing No.
Sheet 4 of 4

Existing Ground
Proposed HM

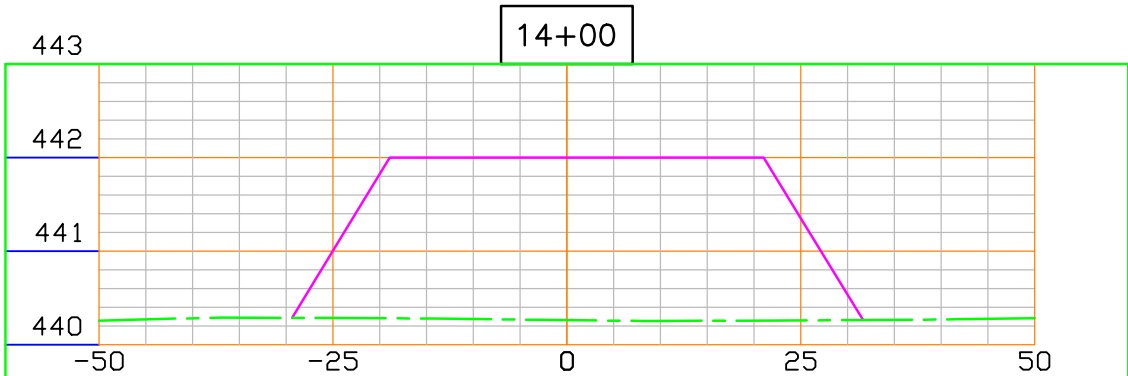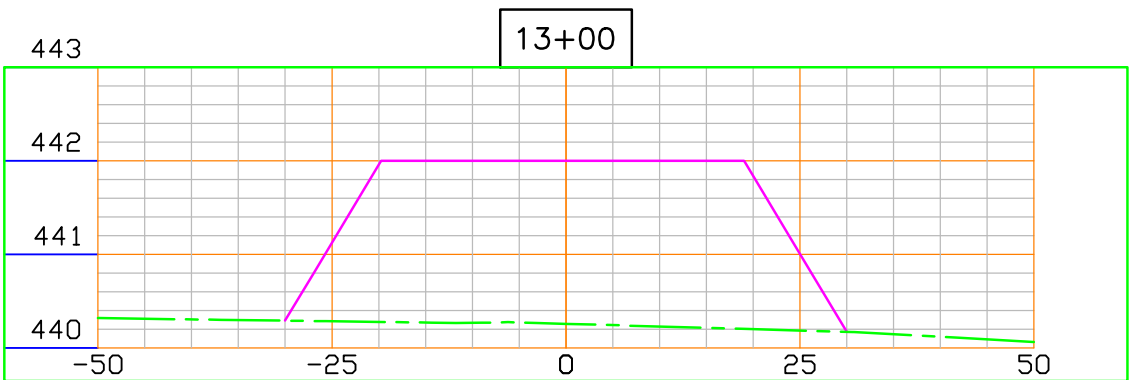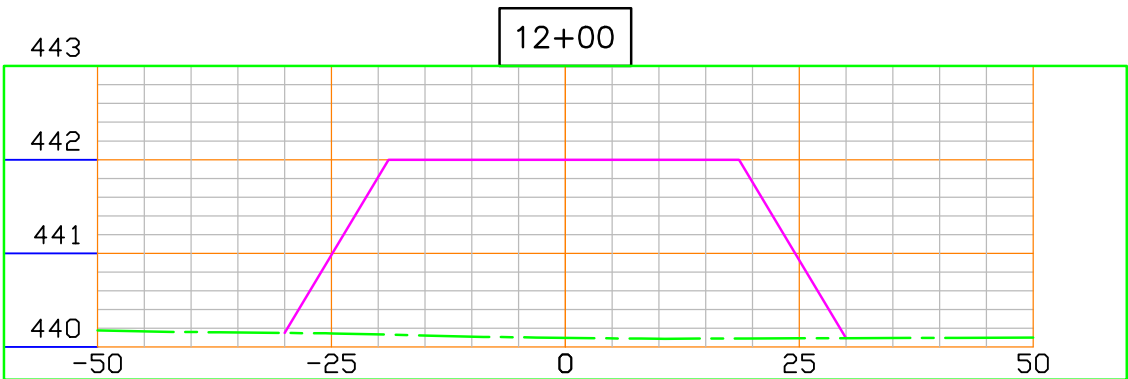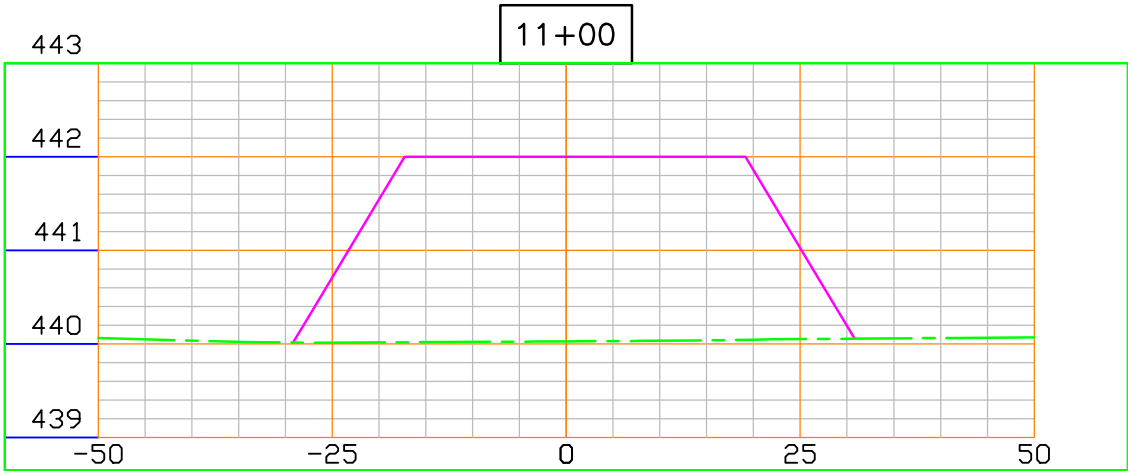

File No.	 United States Department of Agriculture Natural Resources Conservation Service	HM9A X-SECTIONS (1) Daugherty Wetland			Date
Drawing No.					Designed <u>Kerry Bushue</u> <u>10/23/23</u>
Sheet <u>###</u> of <u>###</u>					Drawn <u>Kerry Bushue</u> <u>10/23/23</u>
					Checked <u>M. Dasenbrock</u> <u>8.2025</u>
		York Twnshp, .	Sec 27	T 9 N R 11 W	Clark County County, IL.
					Approved <u>M. Dasenbrock</u> <u>8.2025</u>

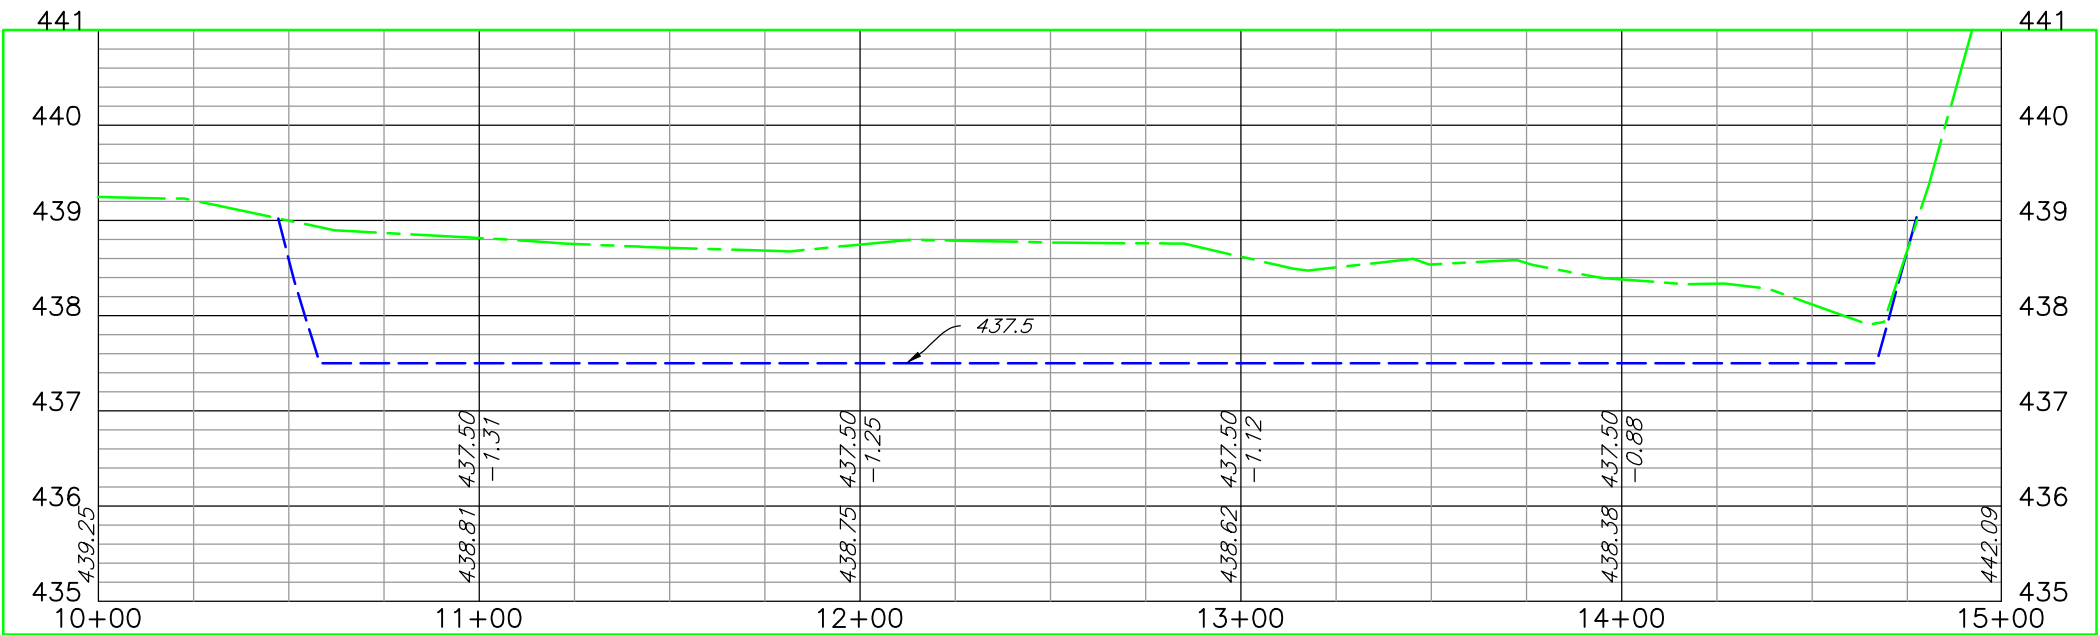

Existing Ground
Proposed Pool






File No.
Drawing No.
Sheet # of #

POOL B1 PROFILE
Daugherty Wetland

Designed Kerry Bushue 10/23/23
Drawn Kerry Bushue 10/23/23
Checked M. Daenbroeck 8/2025
Approved M. Daenbroeck 8/2025

York Twnshp. . Sec27 T 9N R 11W Clark County, IL.


Existing Ground
Proposed Pool

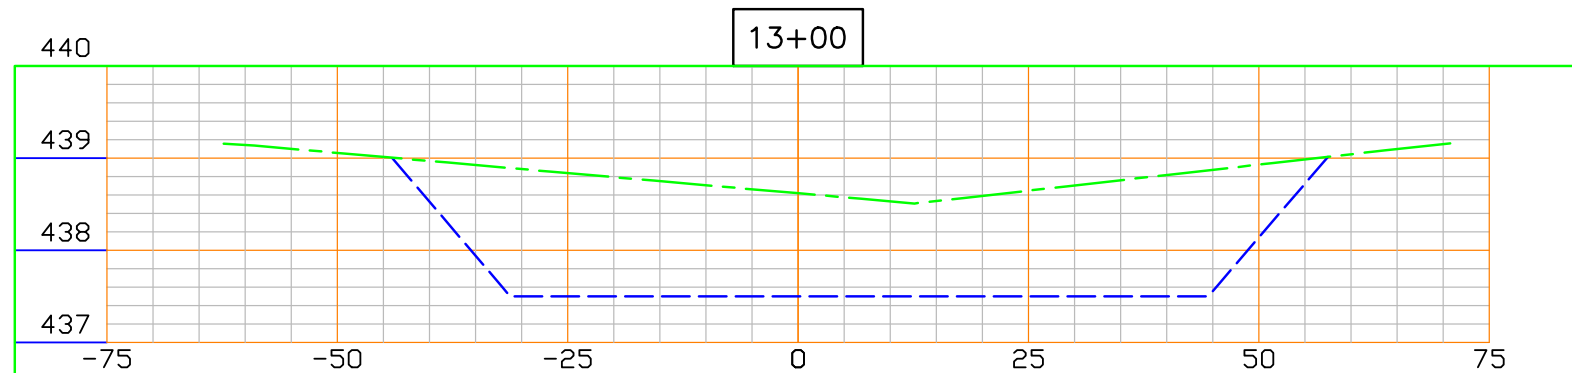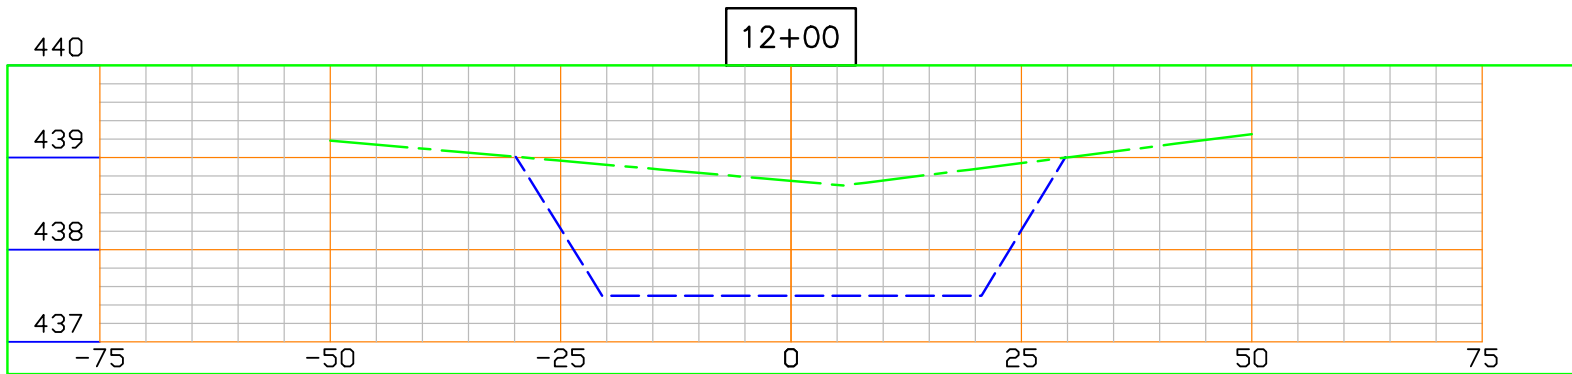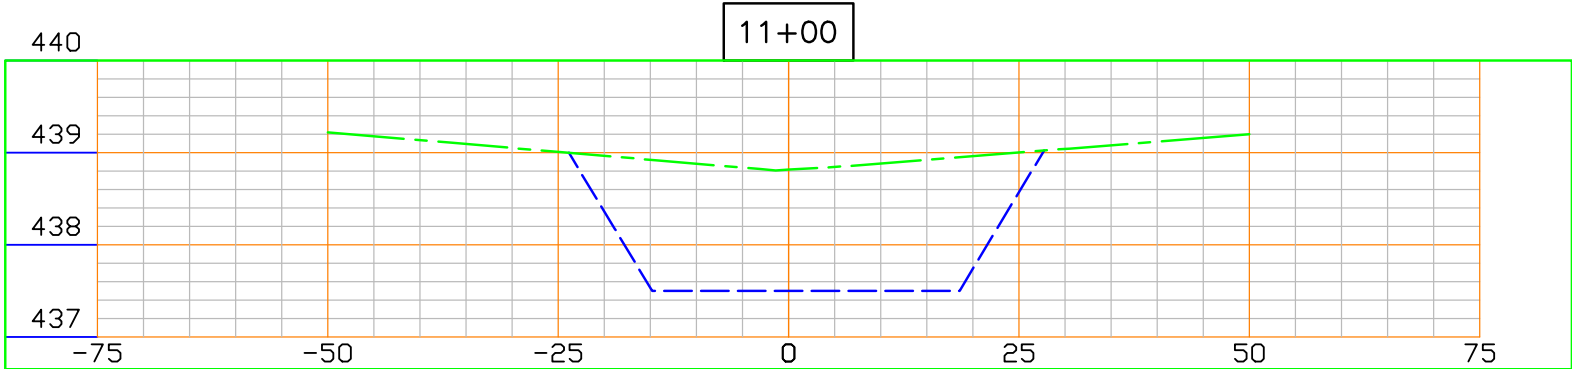



File No.	 United States Department of Agriculture Natural Resources Conservation Service	POOL B1 X-SECTIONS (1) Daugherty Wetland	Designed <u>Kerry Bushue</u> <u>10/23/23</u> Date			
Drawing No.			Drawn <u>Kerry Bushue</u> <u>10/23/23</u>			
Sheet <u>###</u> of <u>###</u>			Checked <u>M. Dasenbrock</u> <u>8.2025</u>			
York Twnshp, .		Sec 27	T 9 N	R 11 W	Clark County County, IL.	Approved <u>M. Dasenbrock</u> <u>8.2025</u>

Existing Ground

Proposed Pool

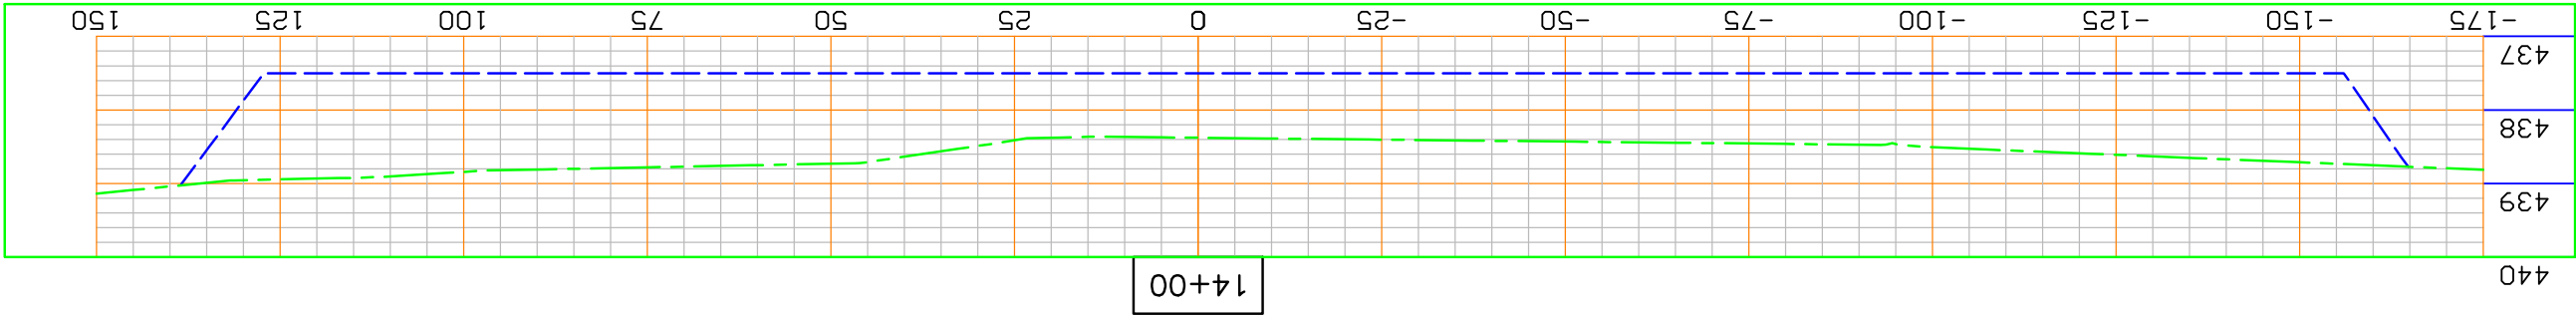

File No.		United States Department of Agriculture	POOL B1 X-SECTIONS (2) Daugherty Wetland	Designed	Kerry Bushue	Date	10/23/23			
				Drawn	Kerry Bushue	10/23/23				
				Checked	M. Dasenbrock	8/20/25				
Sheet ## of .			York Twnshp, .	Sec 27	T 9N	R 11W	Clark County County, IL.	Approved	M. Dasenbrock	8/20/25

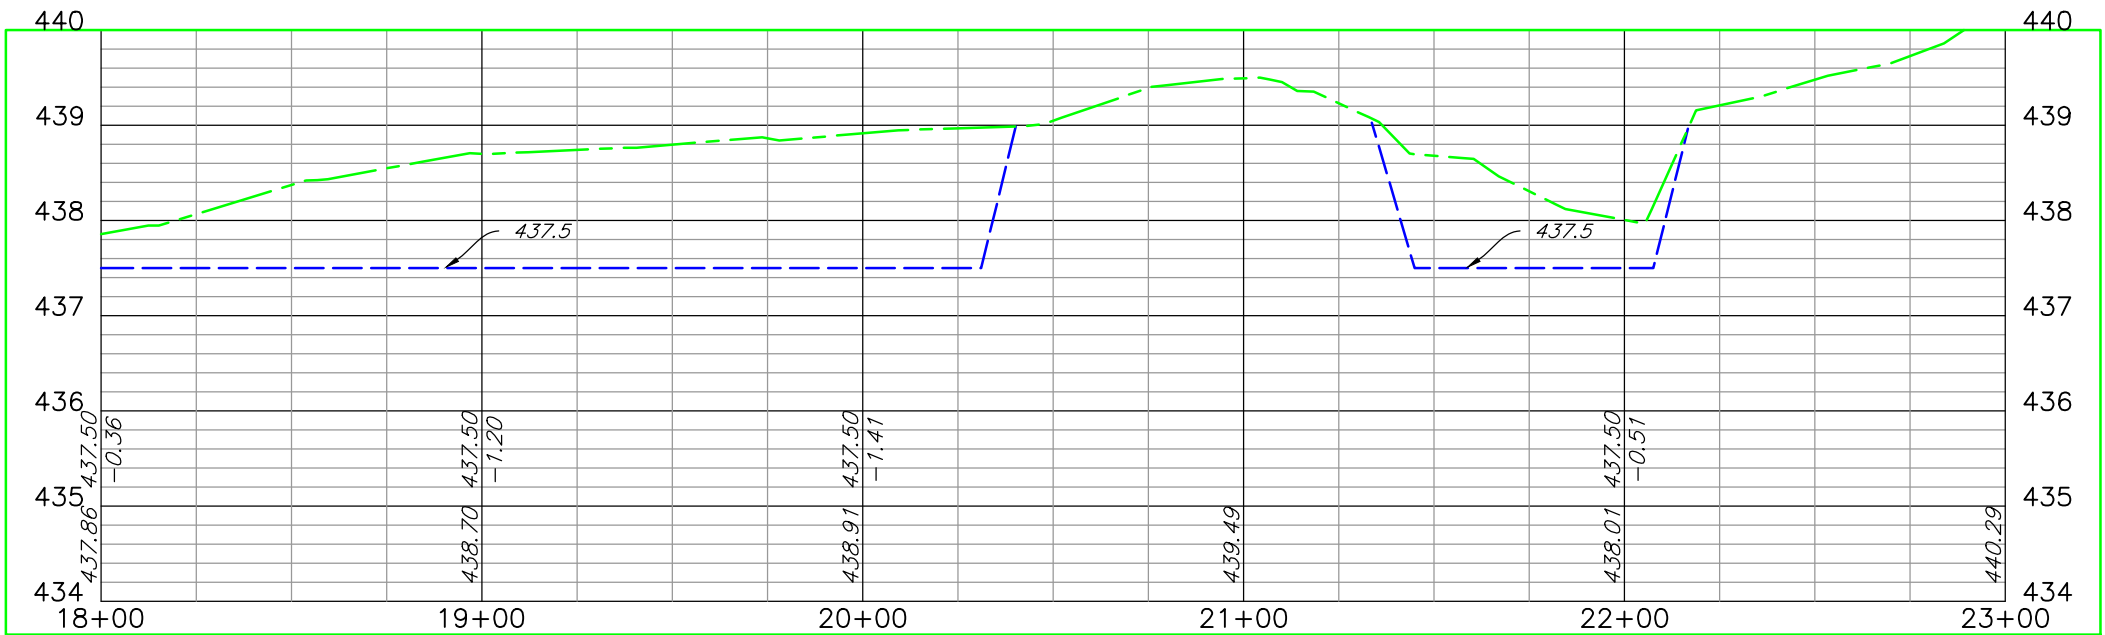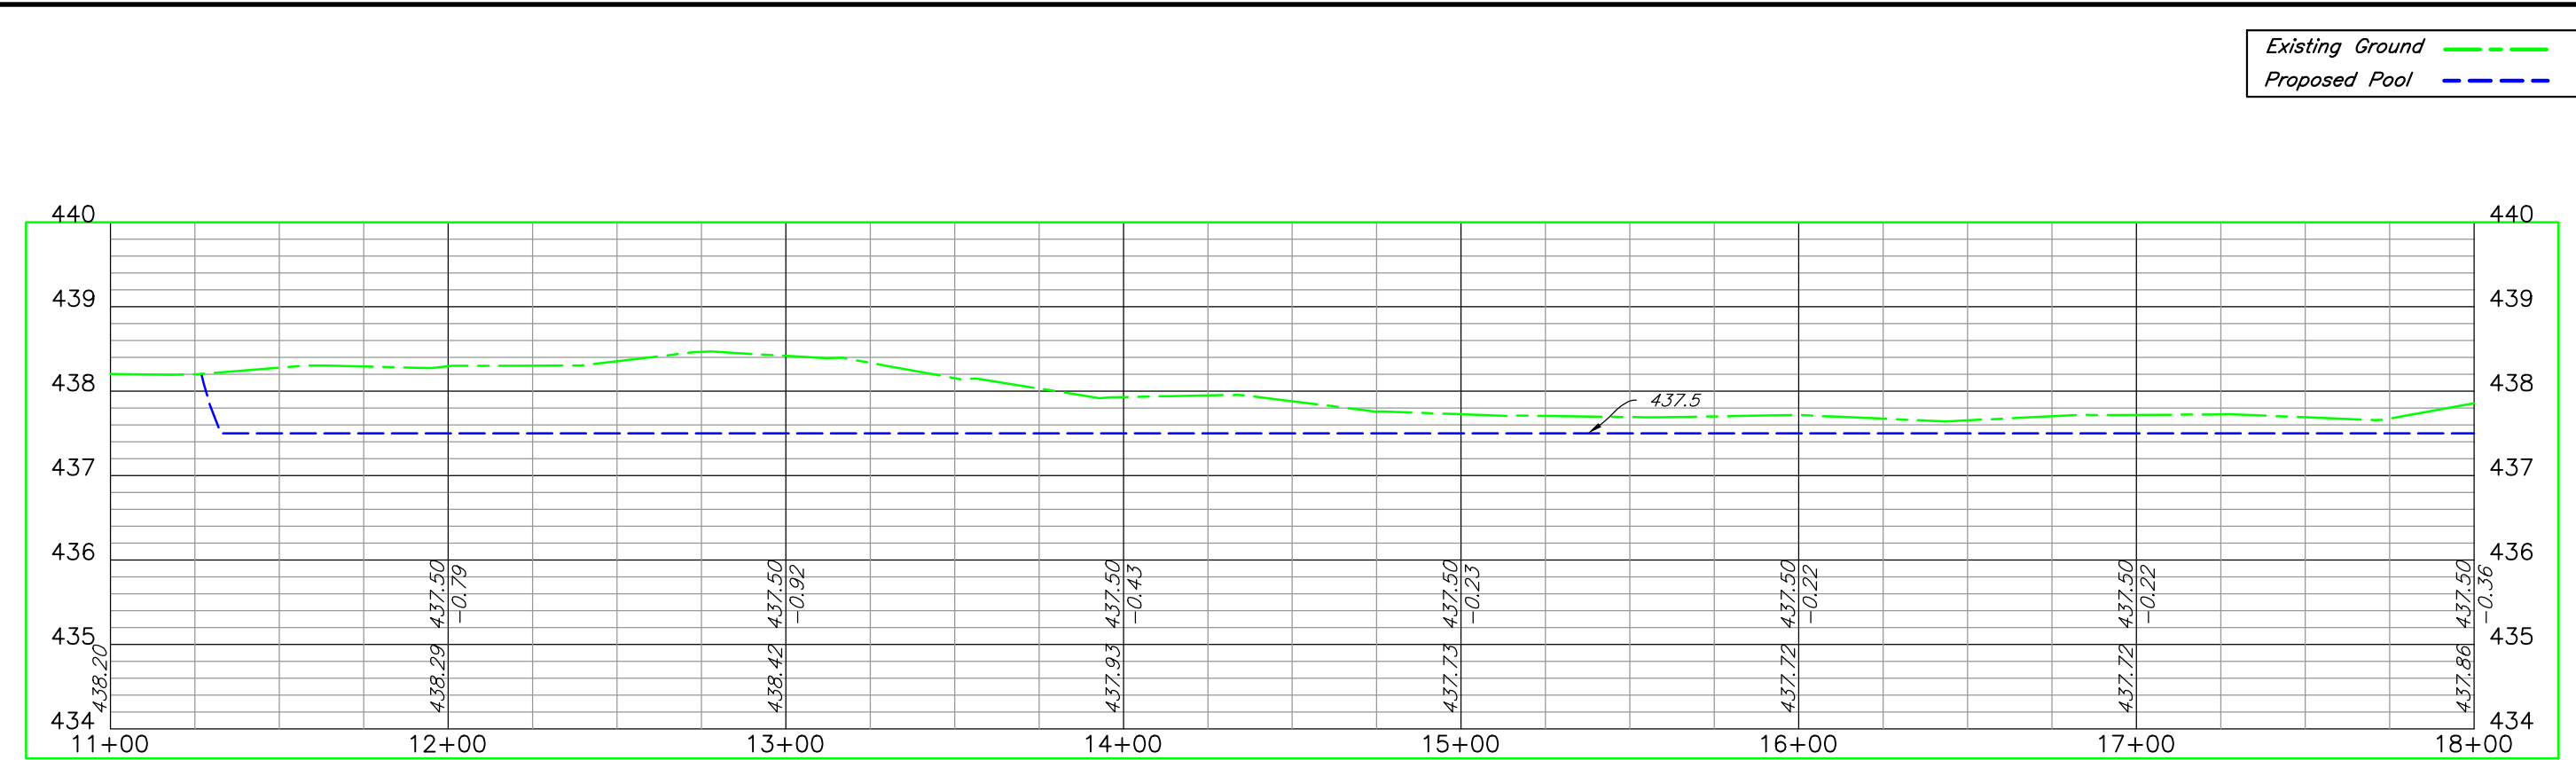

United States
Department of
Agriculture

Natural Resources
Conservation Service

File No. _____

Drawing No. _____


Sheet 4 of 4

POOL B2 PROFILE
Daugherty Wetland


Designed Kerry Bushue 10/23/23
 Drawn Kerry Bushue 10/23/23
 Checked M. Dasenbrock 8.2025
 Approved M. Dasenbrock 8.2025

York Twnshp, . Sec27 T 9N R 11W Clark County County, IL


Existing Ground
Proposed Pool

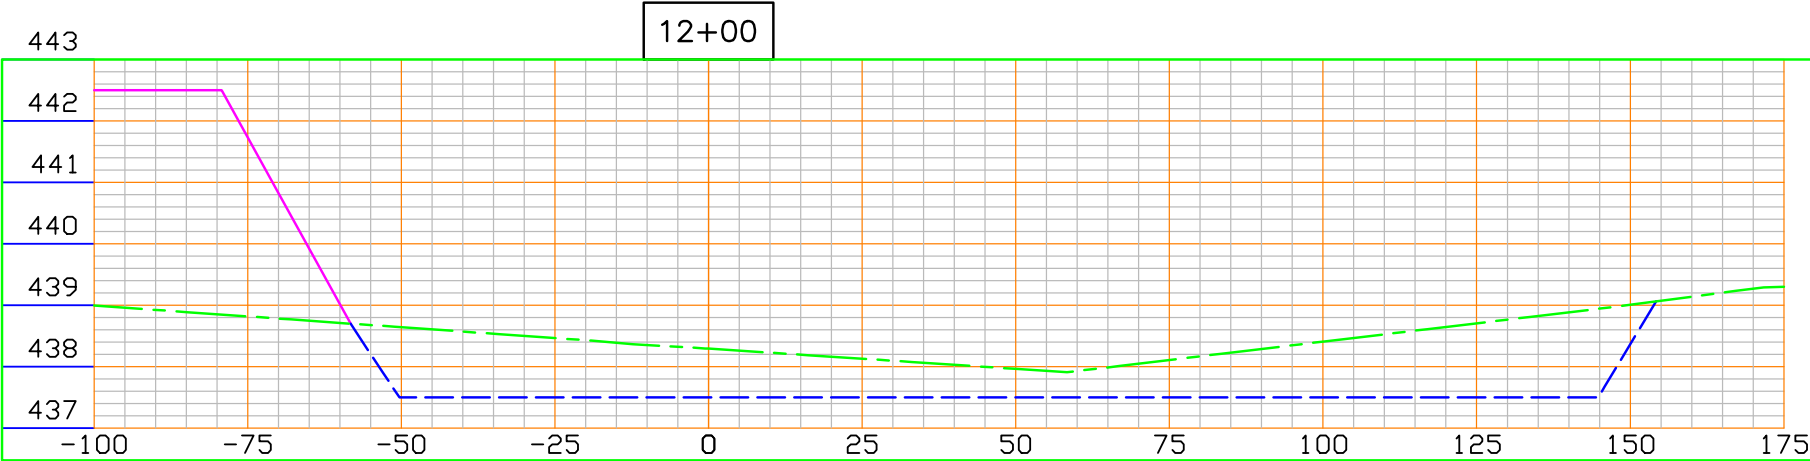






16+00

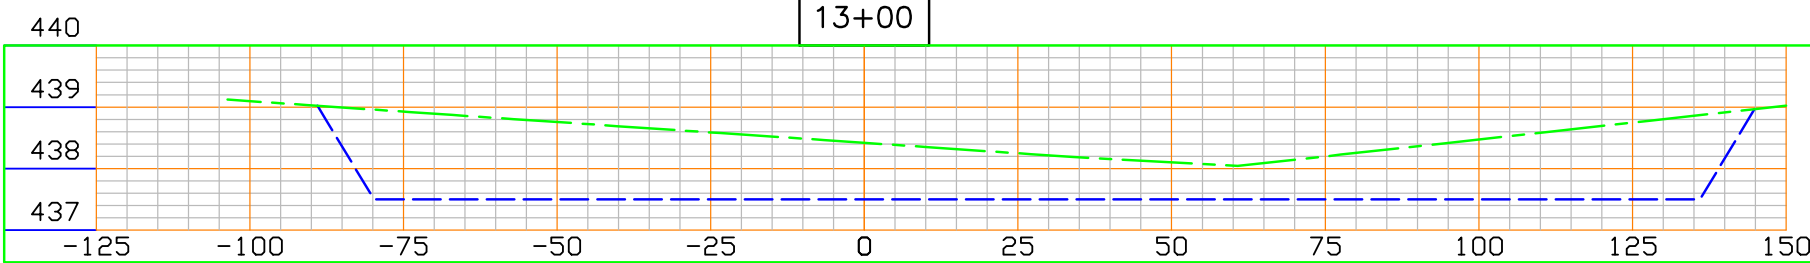





14+00

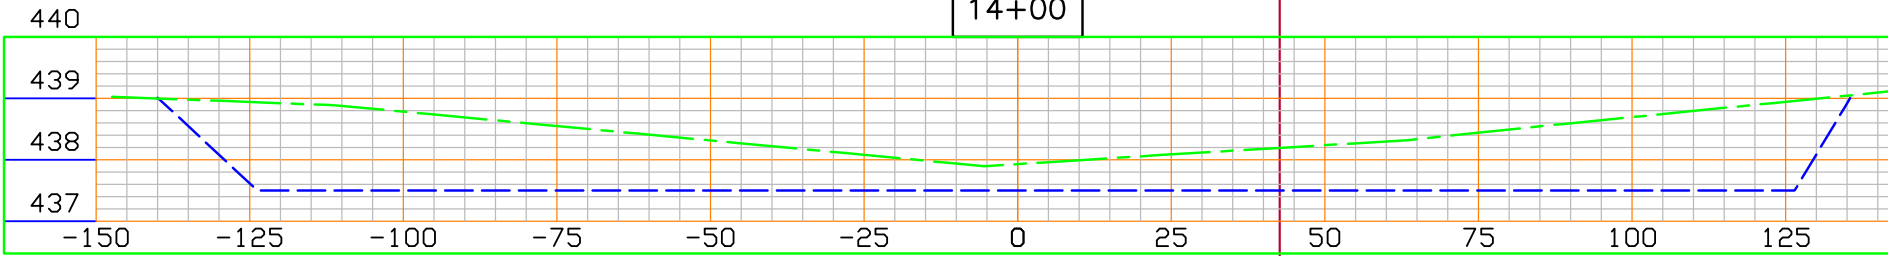


File No.	 United States Department of Agriculture Natural Resources Conservation Service	POOL B2 X-SECTIONS (1) Daugherty Wetland	York Twnshp, . Sec27 T 9N R 11W Clark County County, IL.	Designed <u>Kerry Bushue</u> <u>10/23/23</u>
Drawing No.				Drawn <u>Kerry Bushue</u> <u>10/23/23</u>
Sheet <u>###</u> of <u>.</u>				Checked <u>M. Dasenbrock 8.2025</u> Approved <u>M. Dasenbrock 8.2025</u>

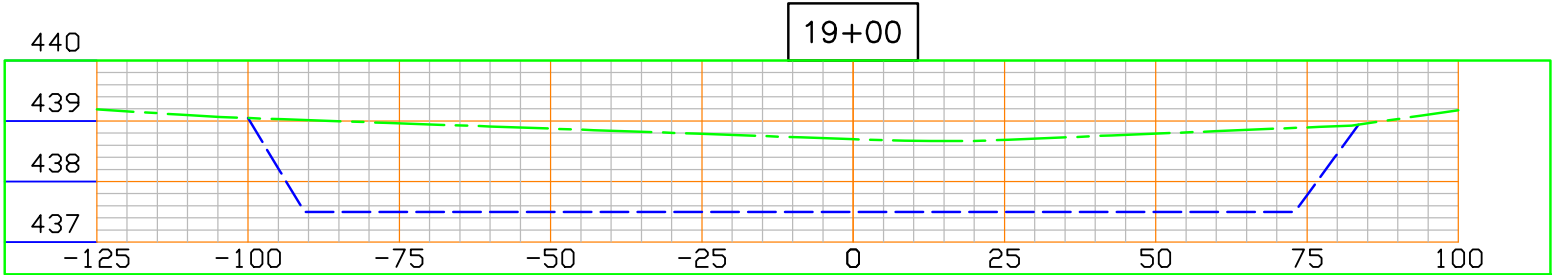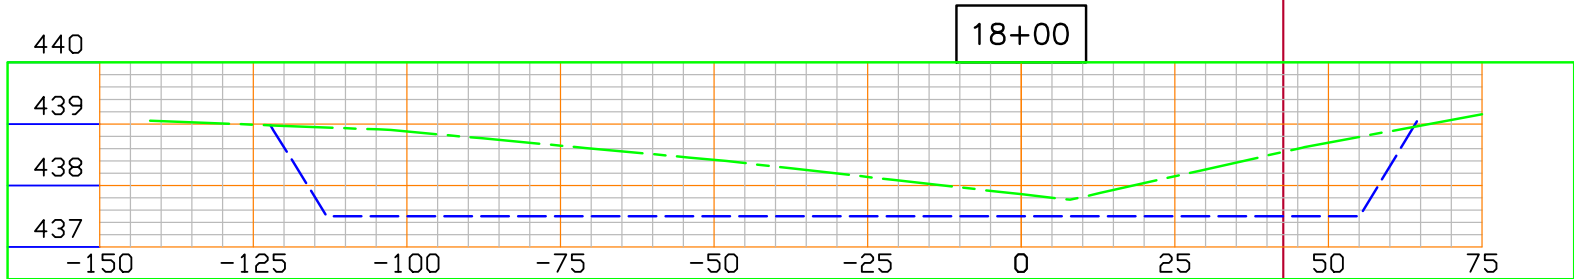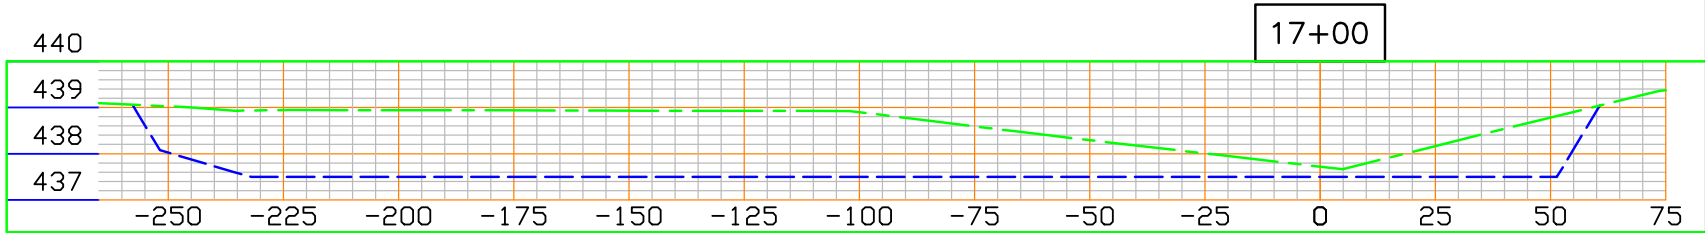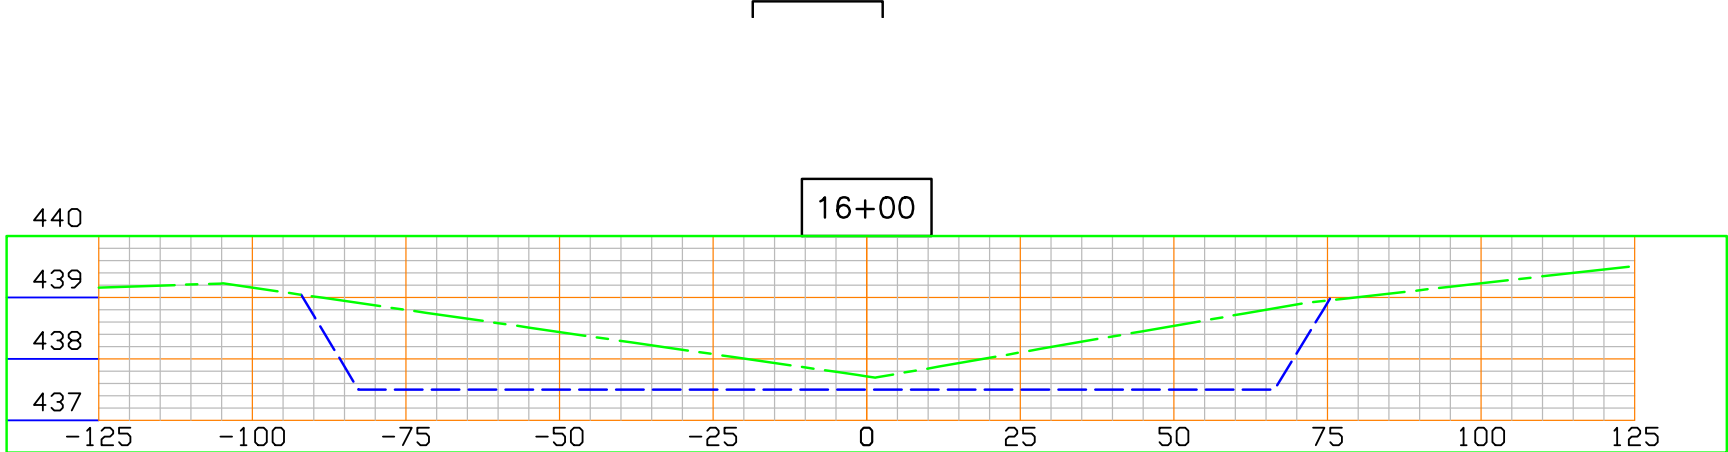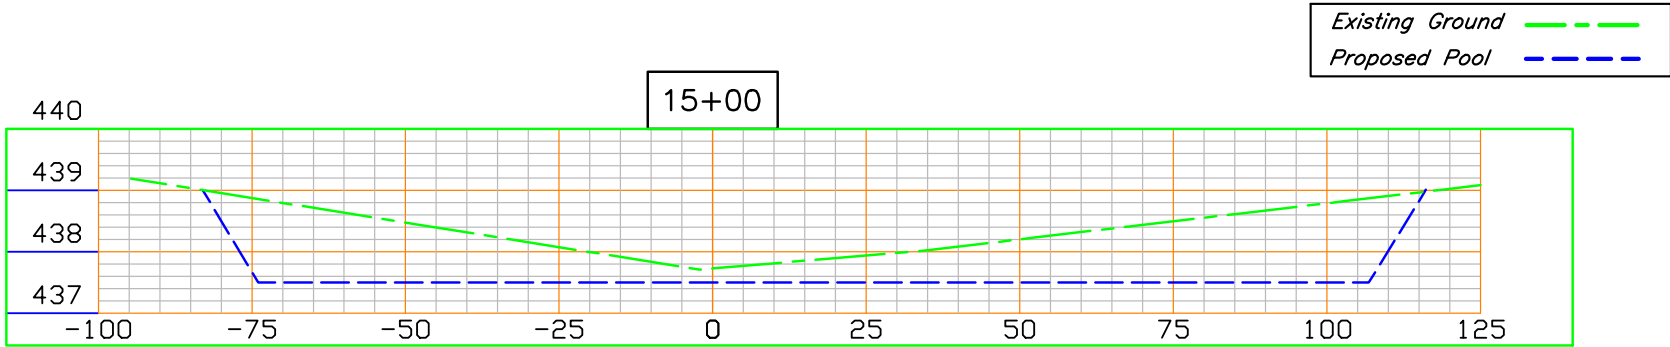

File No.	 United States Department of Agriculture Natural Resources Conservation Service	POOL B2 X-SECTIONS (2) Daugherty Wetland				Designed <u>Kerry Bushue</u> <u>10/23/23</u>
Drawing No.						Drawn <u>Kerry Bushue</u> <u>10/23/23</u>
Sheet <u>###</u> of <u> </u>						Checked <u>M. Dassenbrock 8.2025</u>
						Approved <u>M. Dassenbrock 8.2025</u>
		York Twnshp, . Sec 27 T 9 N R 11 W Clark County County, IL.				

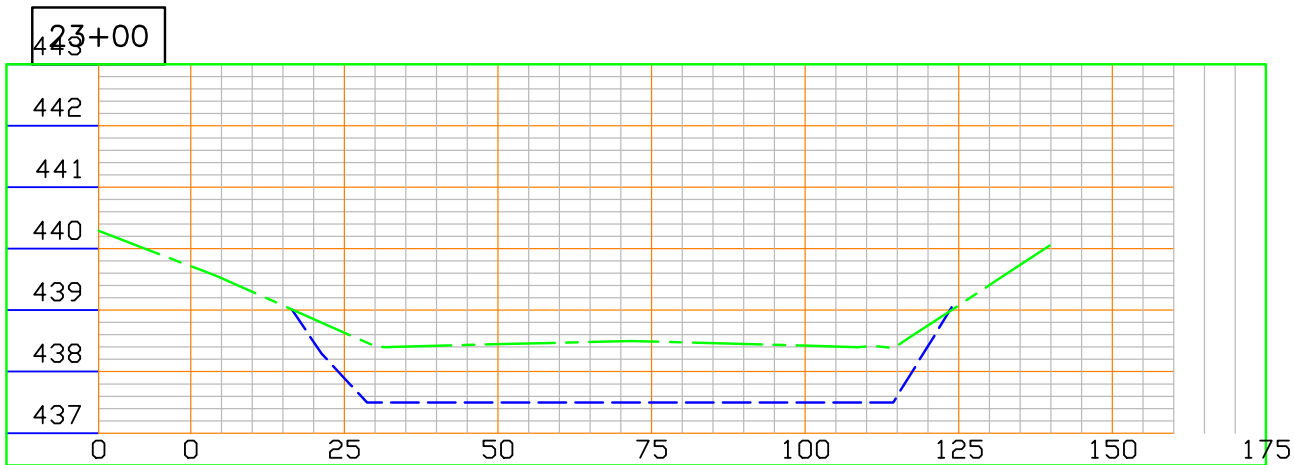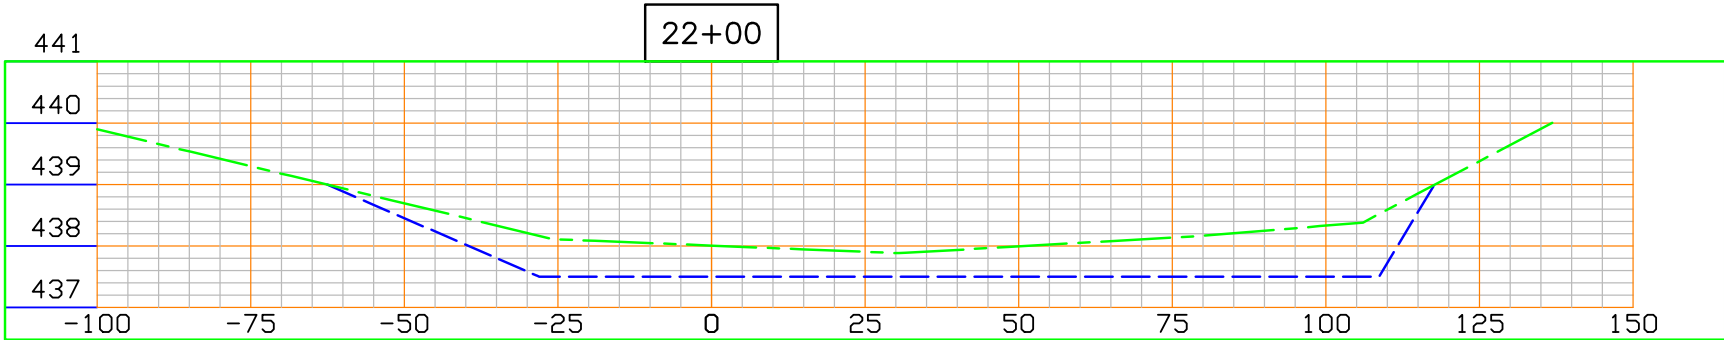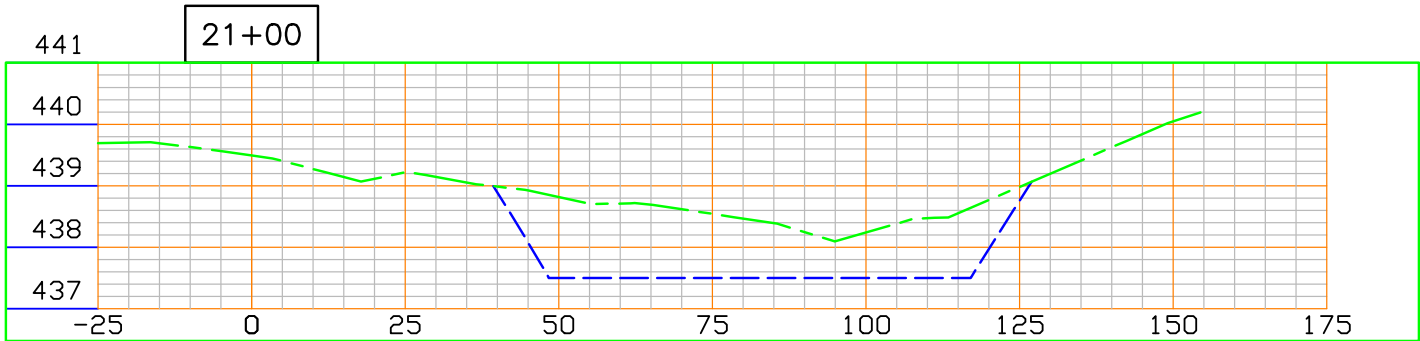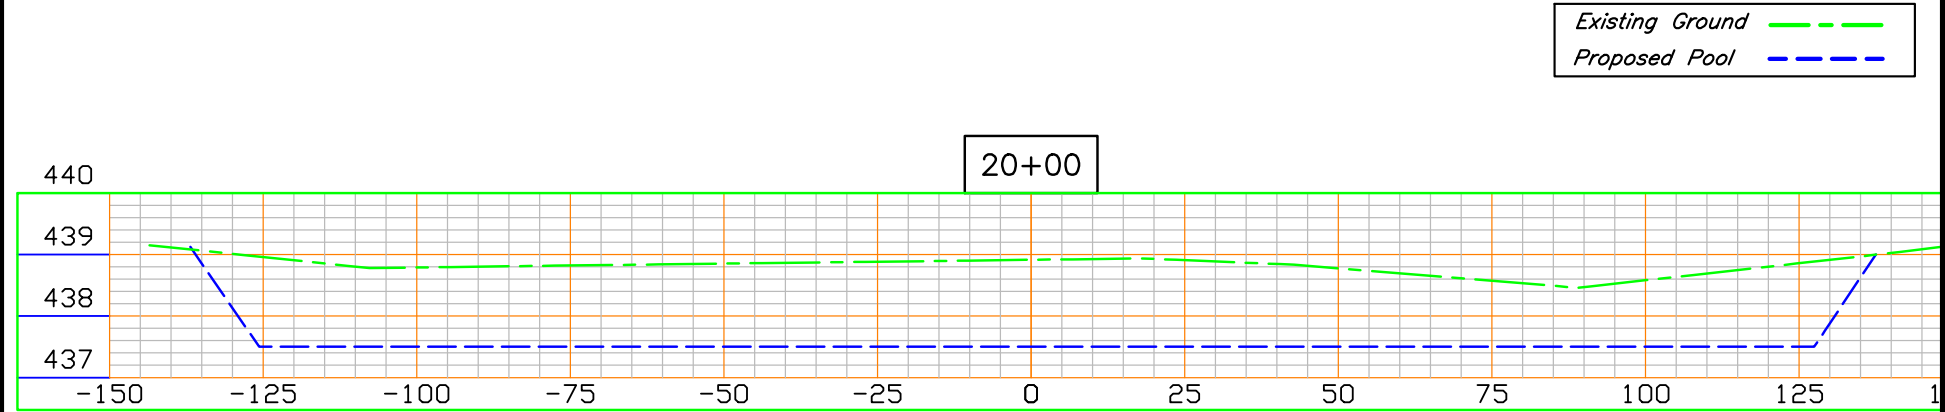

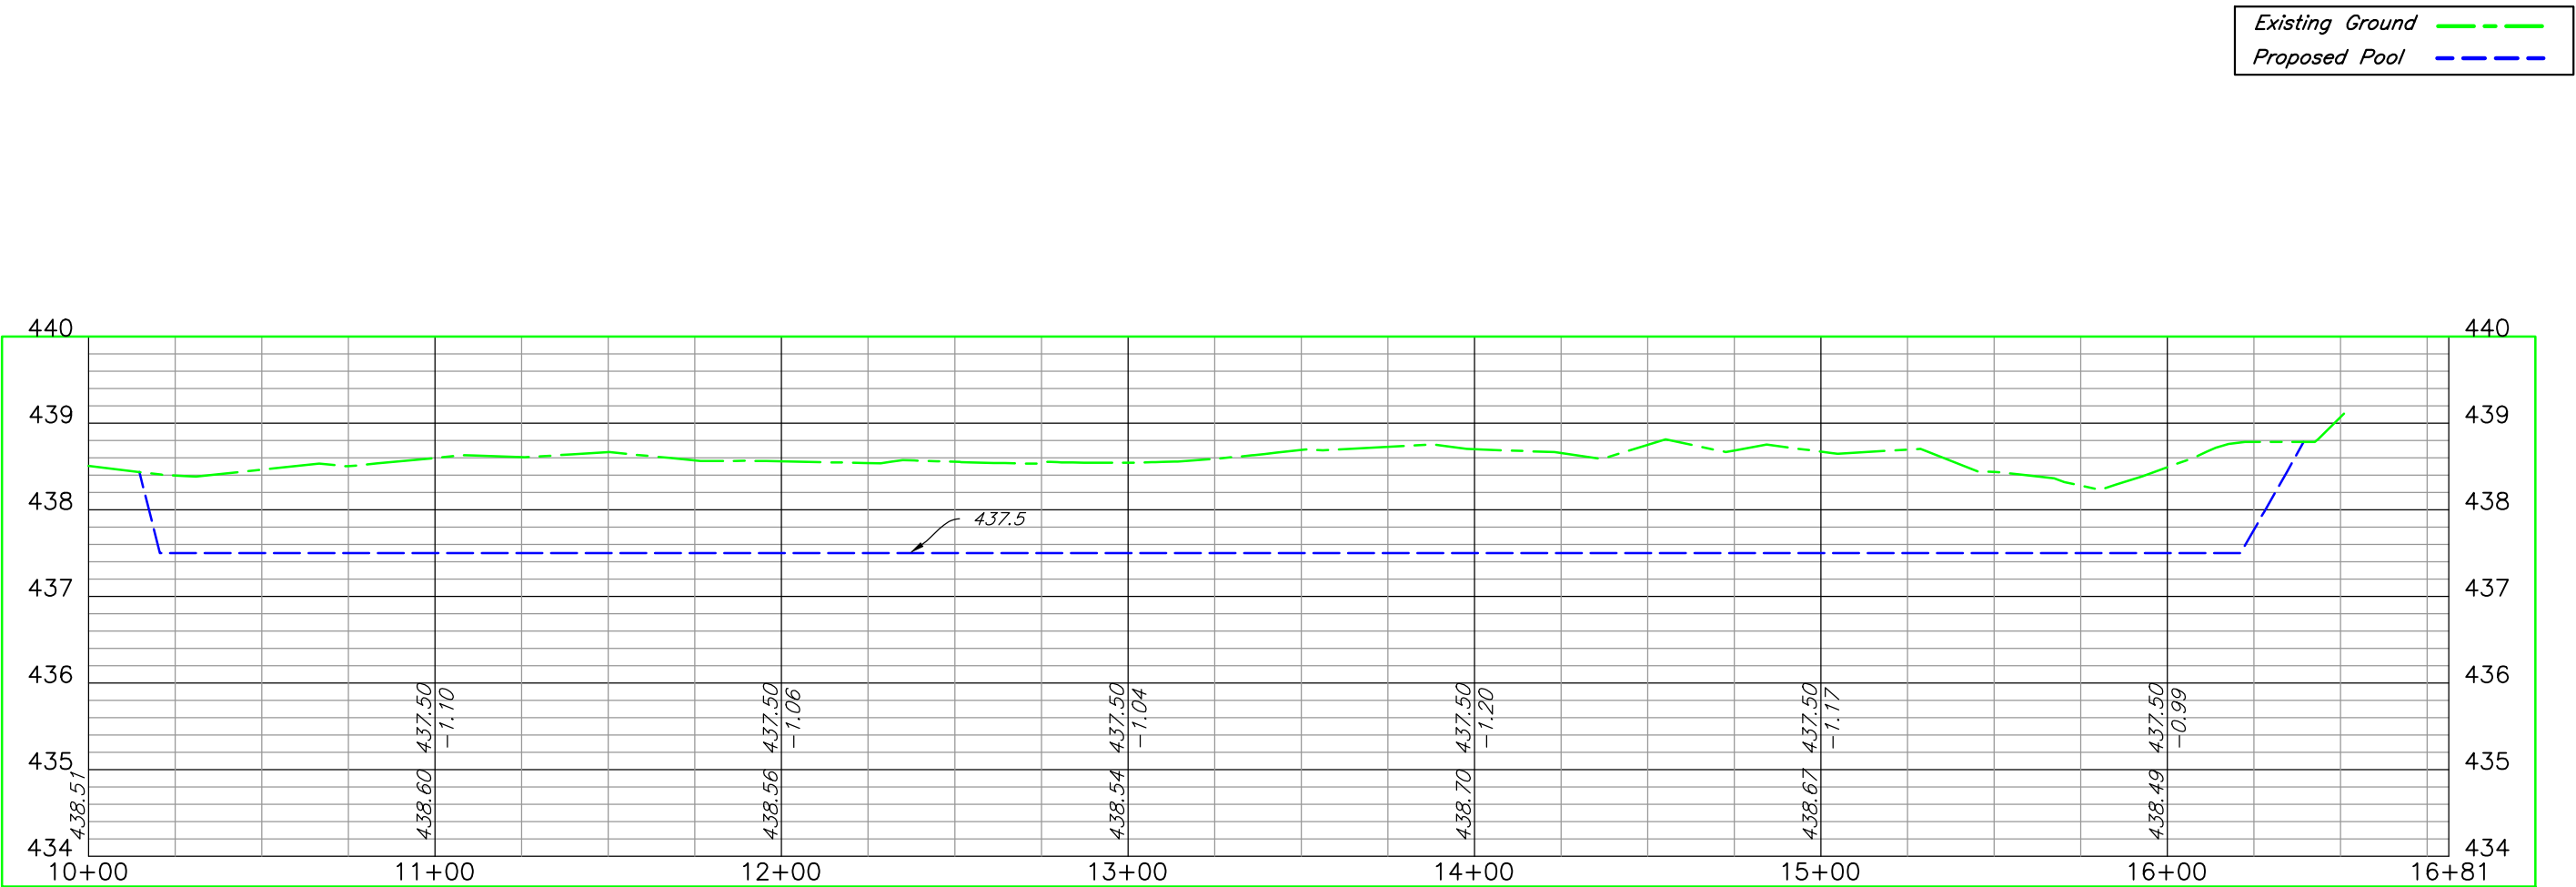





Designed	Kerry Bushue	Date	10/23/23
Drawn	Kerry Bushue	Date	10/23/23
Checked	M. Dasenbrock	Date	8.2025
Approved	M. Dasenbrock	Date	8.2025

POOL C PROFILE
Daugherty Wetland

York Twnshp, . Sec27 T 9N R 11W Clark County County, IL.



United States Department of Agriculture	Natural Resources Conservation Service
File No.	
Drawing No.	
Sheet ### of .	


Existing Ground
Proposed Pool

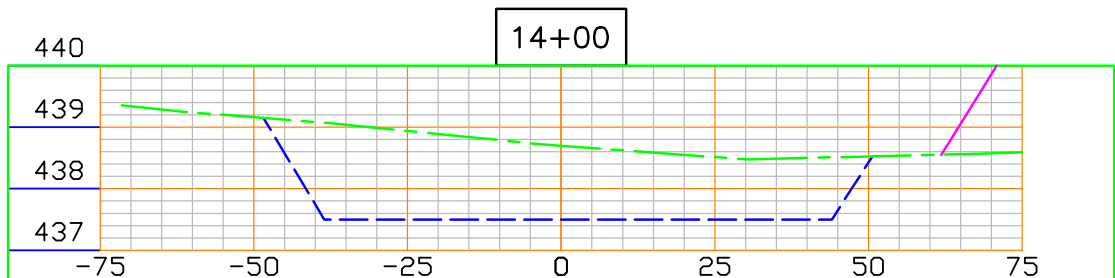
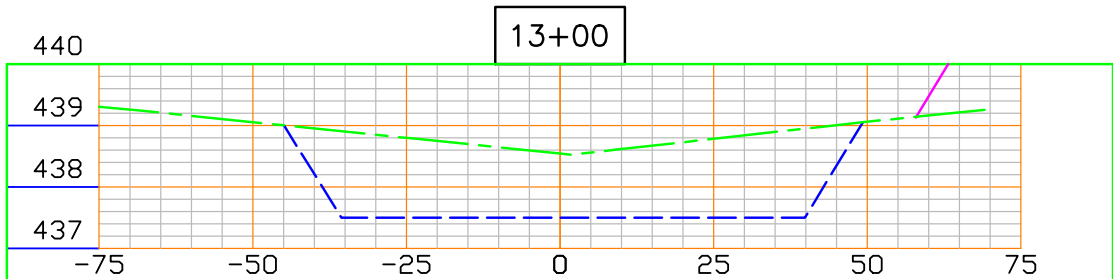
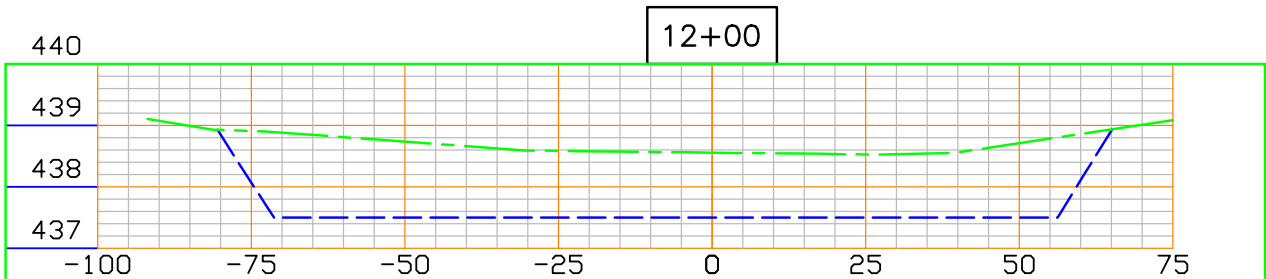
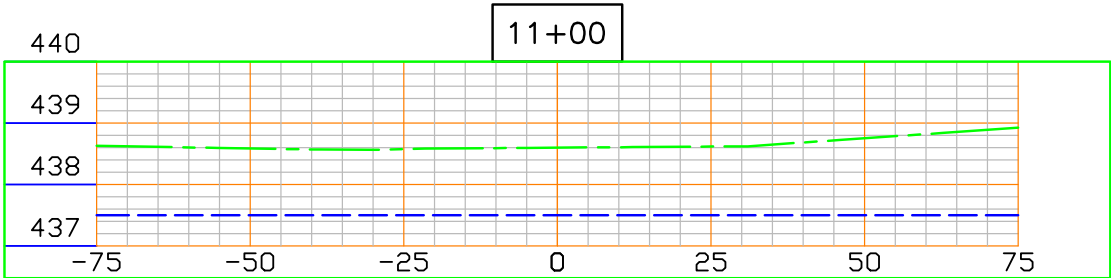






File No.	 United States Department of Agriculture Natural Resources Conservation Service	POOL C X-SECTIONS (1) Daugherty Wetland	Designed <u>Kerry Bushue</u> <u>10/23/23</u>
Drawing No.			Drawn <u>Kerry Bushue</u> <u>10/23/23</u>
Sheet <u>###</u> of <u>###</u>			Checked <u>M. Dasenbrock 8.2025</u>
			Approved <u>M. Dasenbrock 8.2025</u>
		York Twnshp, . Sec 27 T 9 N R 11 W Clark County County, IL.	

Existing Ground
Proposed Pool

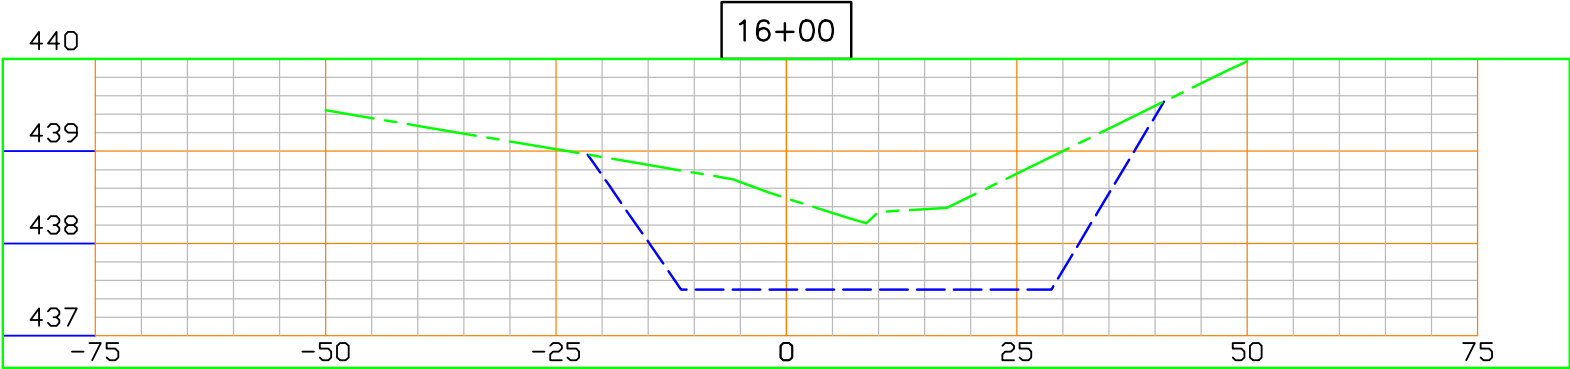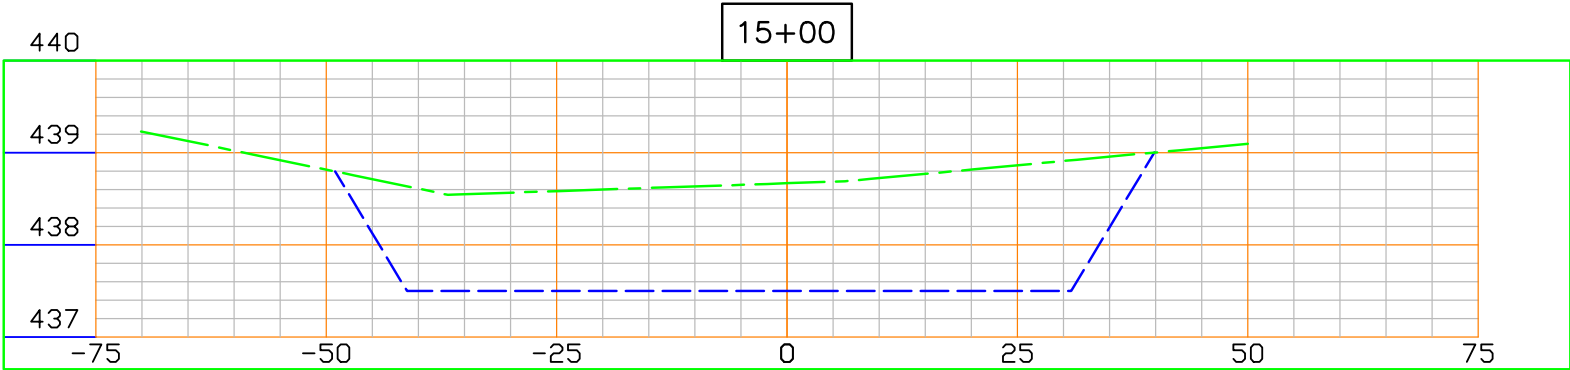

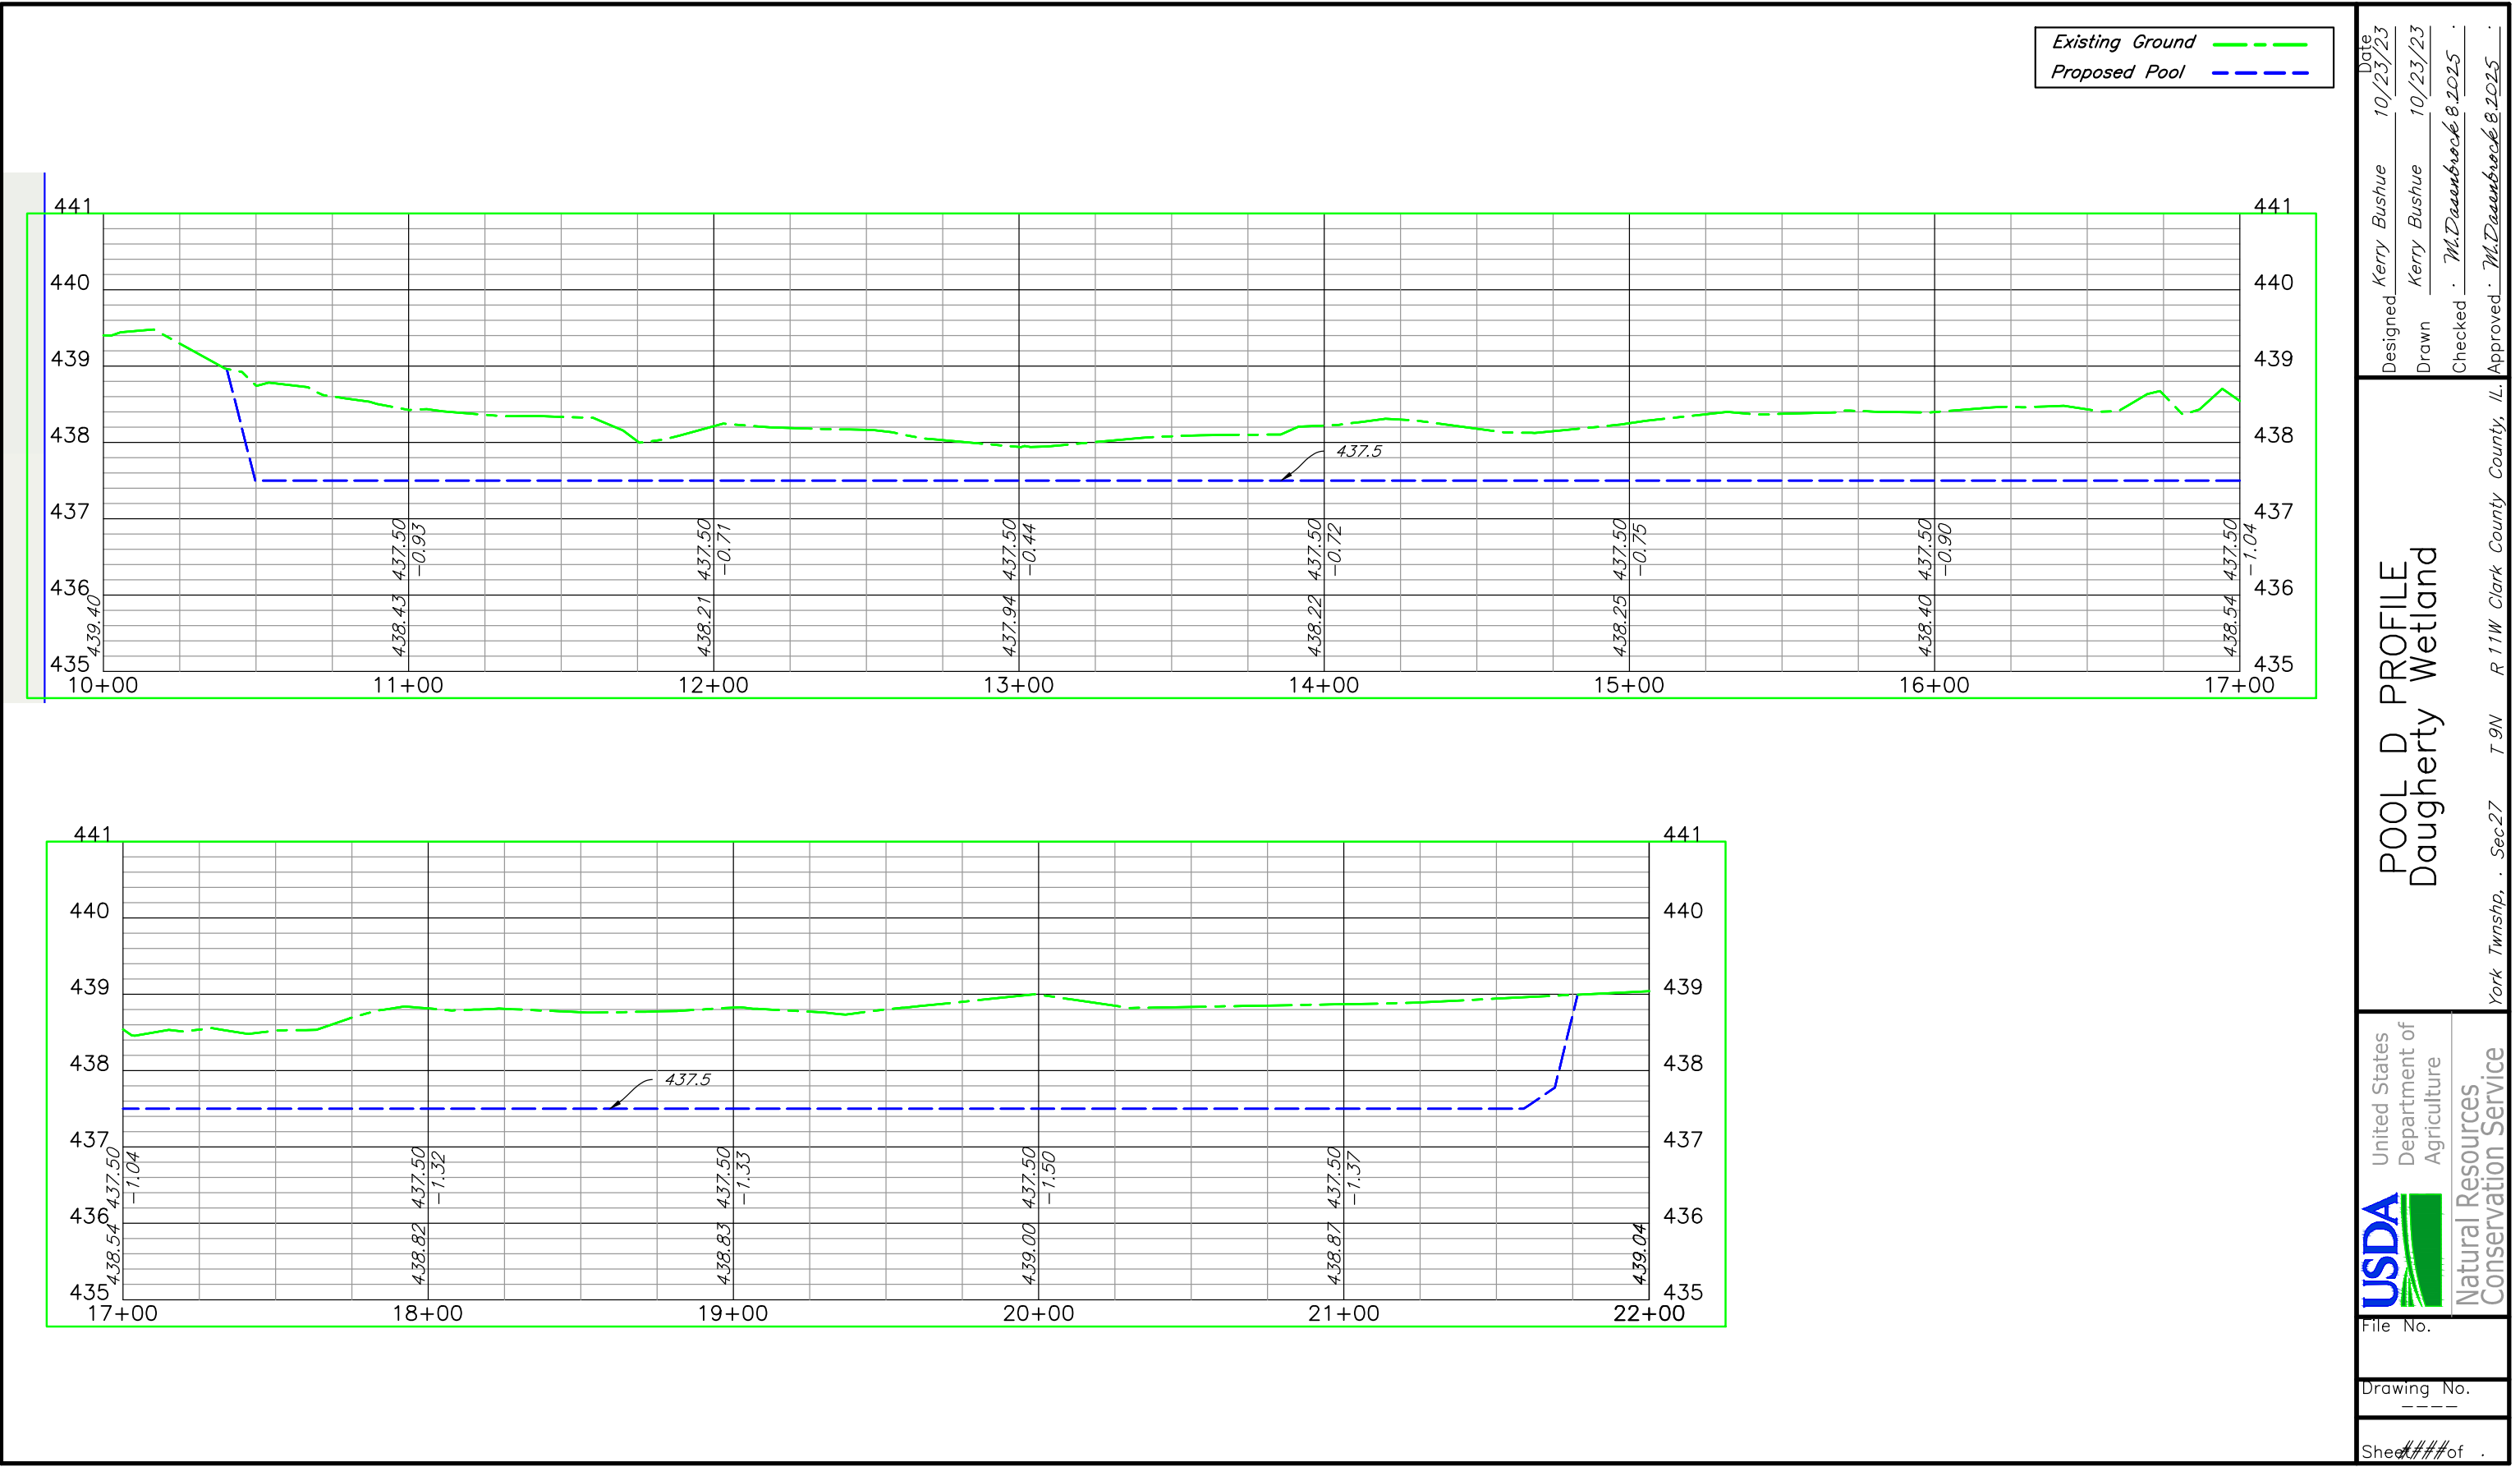

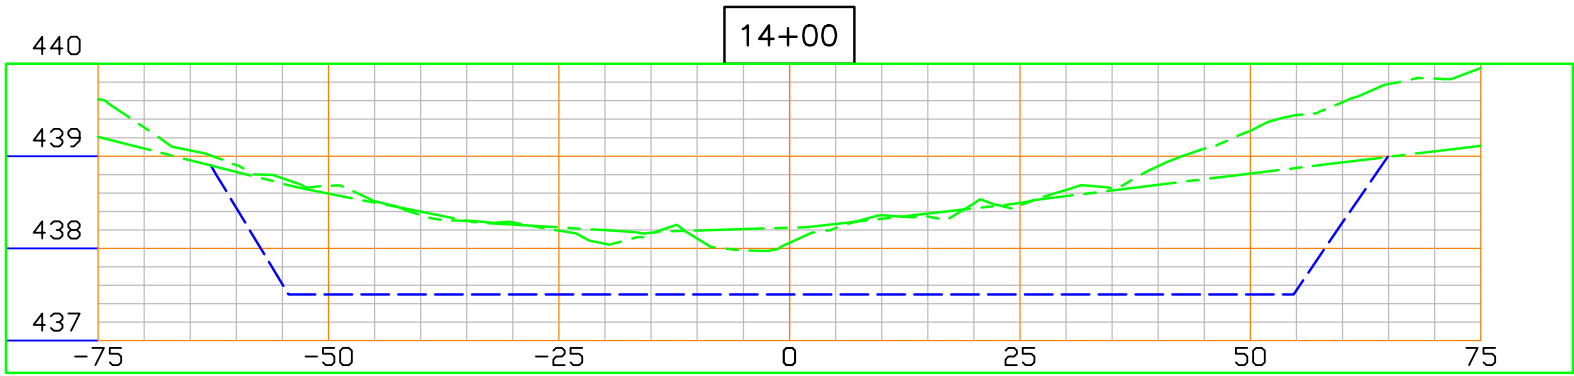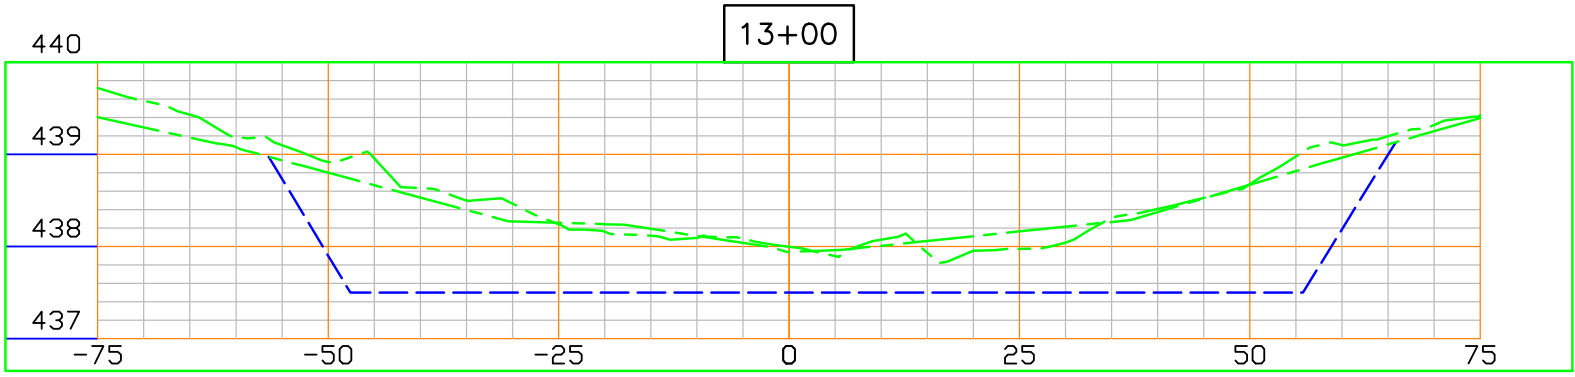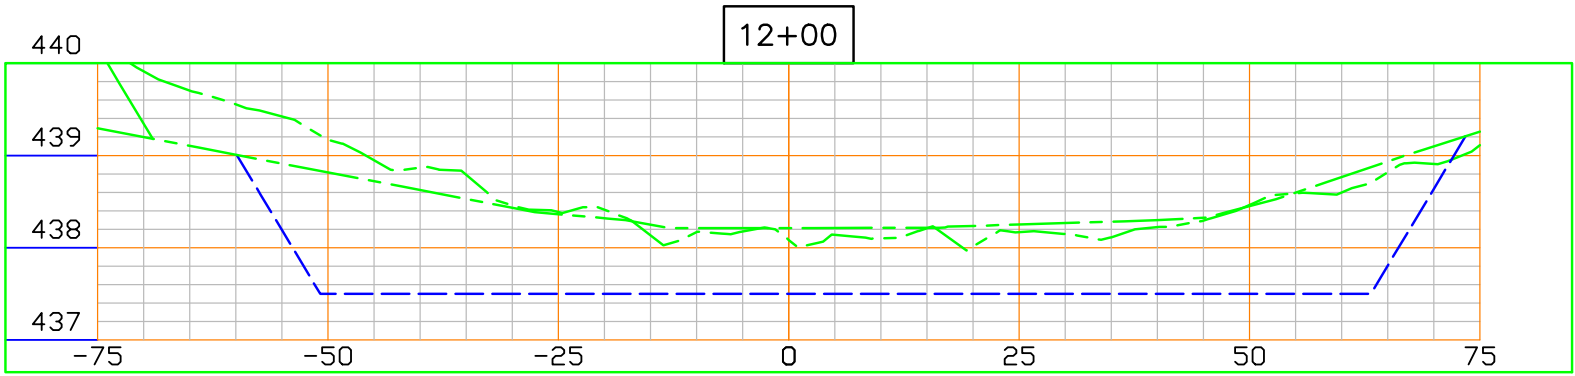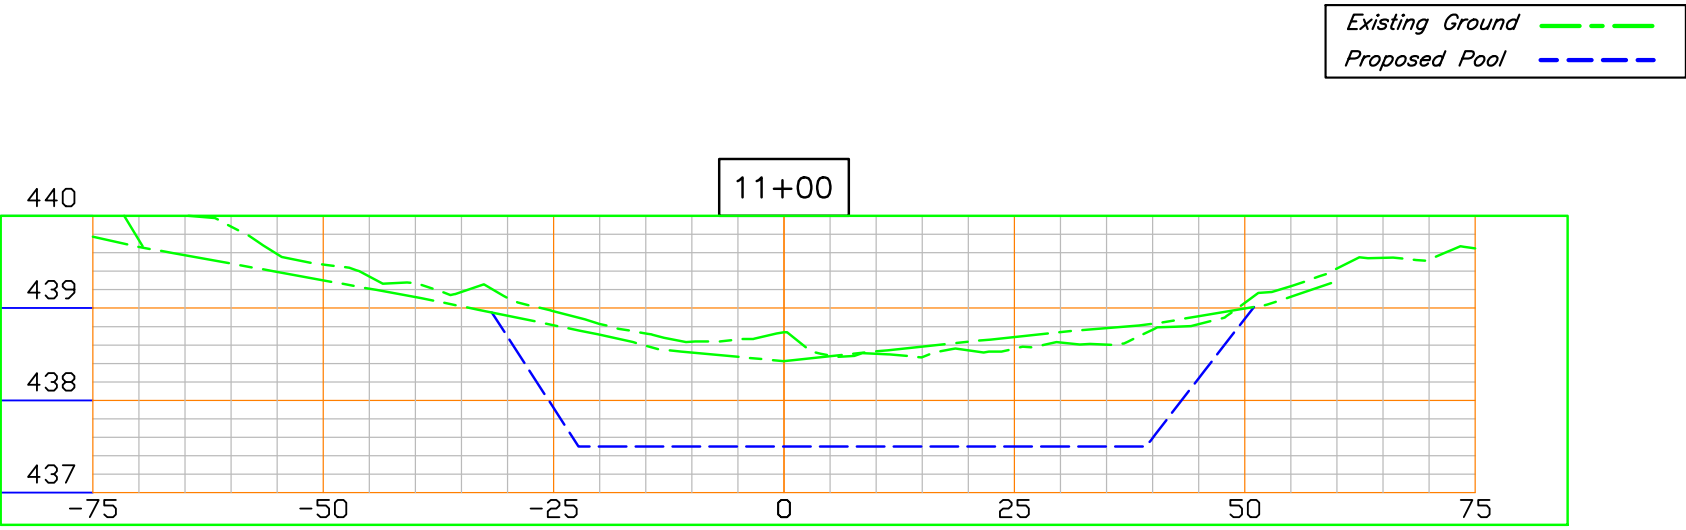

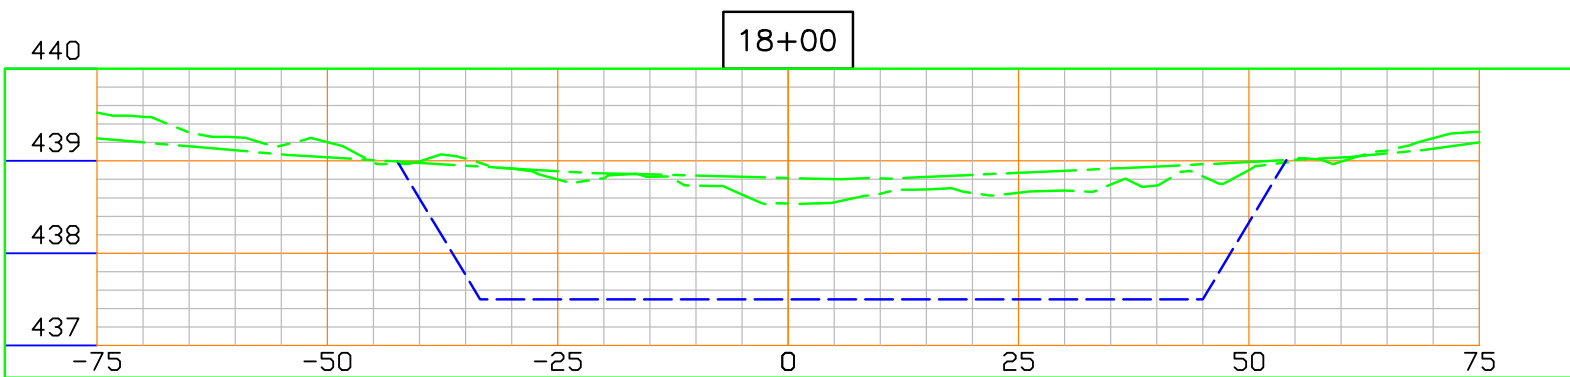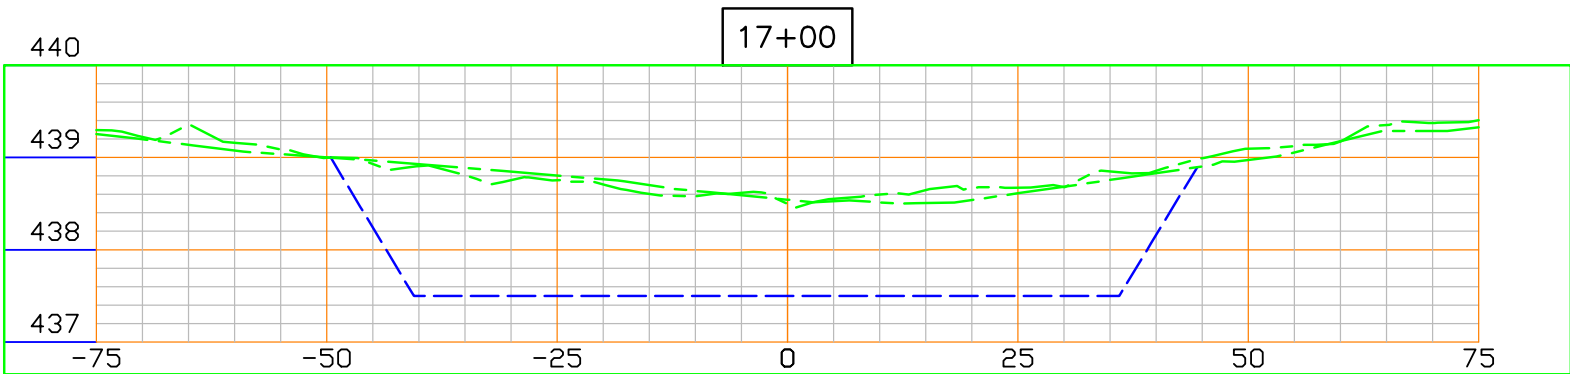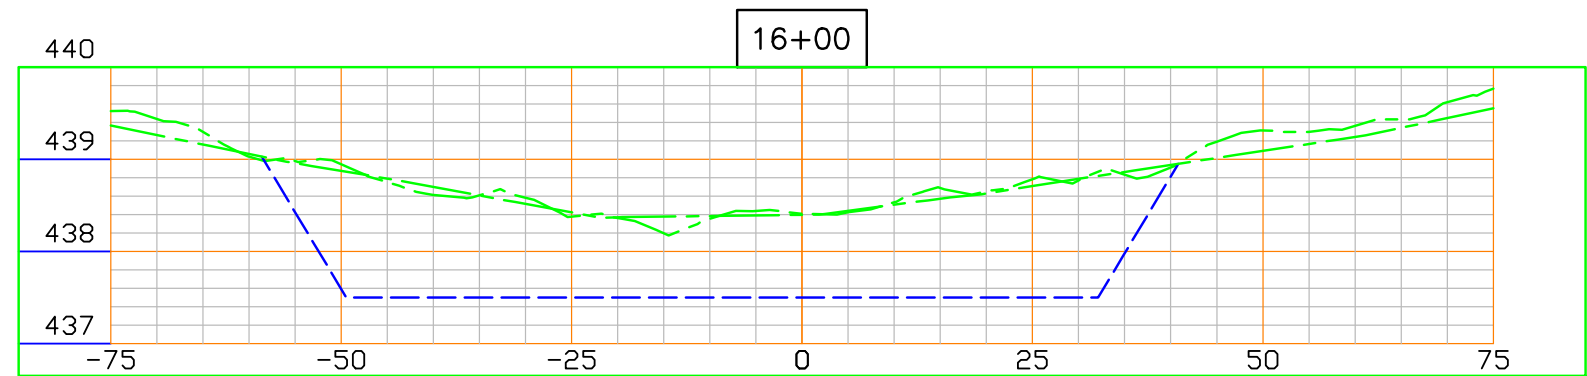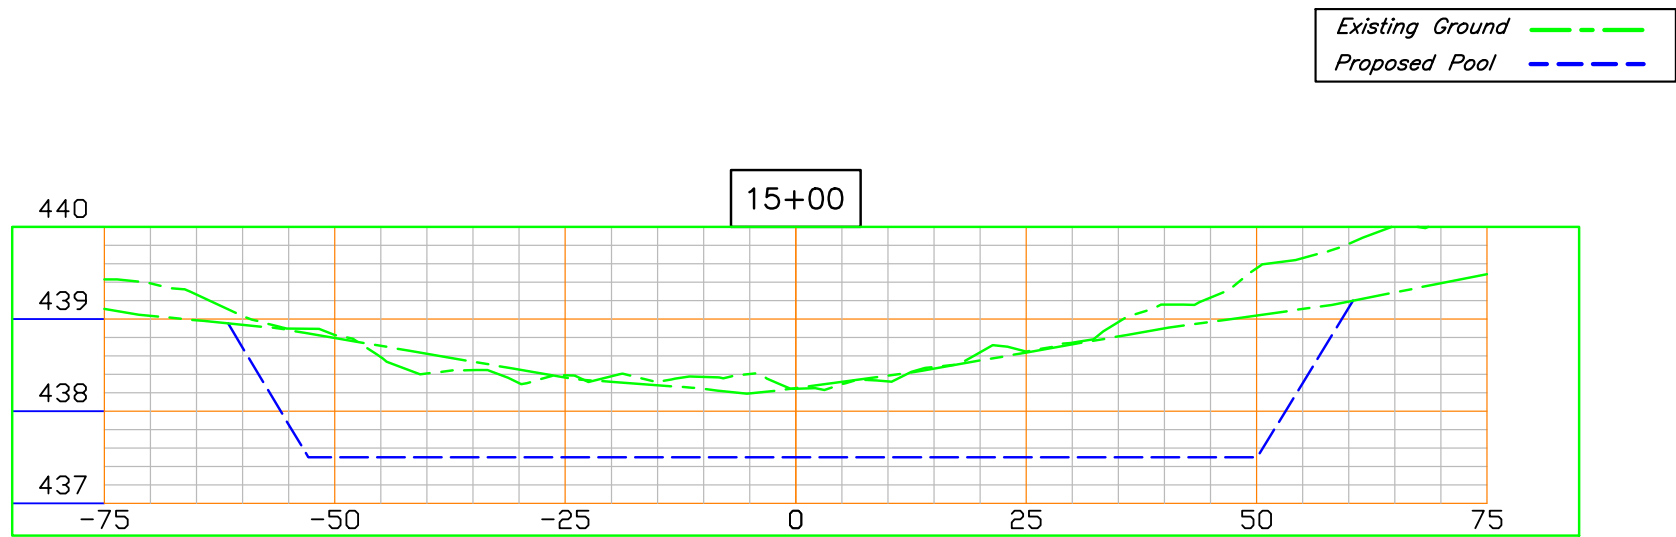

File No.	 United States Department of Agriculture Natural Resources Conservation Service	POOL D X-SECTIONS (2) Daugherty Wetland	Designed <u>Kerry Bushue</u> <u>10/23/23</u>
Drawing No.			Drawn <u>Kerry Bushue</u> <u>10/23/23</u>
Sheet <u>1</u> of <u>1</u>			Checked <u>M. Dasenbrock 8.2025</u>
			Approved <u>M. Dasenbrock 8.2025</u>
		York Twnshp, . Sec 27 T 9 N R 11 W Clark County County, IL.	

