



NORTHERN REGION, REGION 1, DAKOTA PRAIRIE GRASSLANDS, MEDORA RANGER DISTRICT



N/A

02/12/26



R.C.

SHEET TITLE:

SITE PLAN

PROJECT NO. _____

01

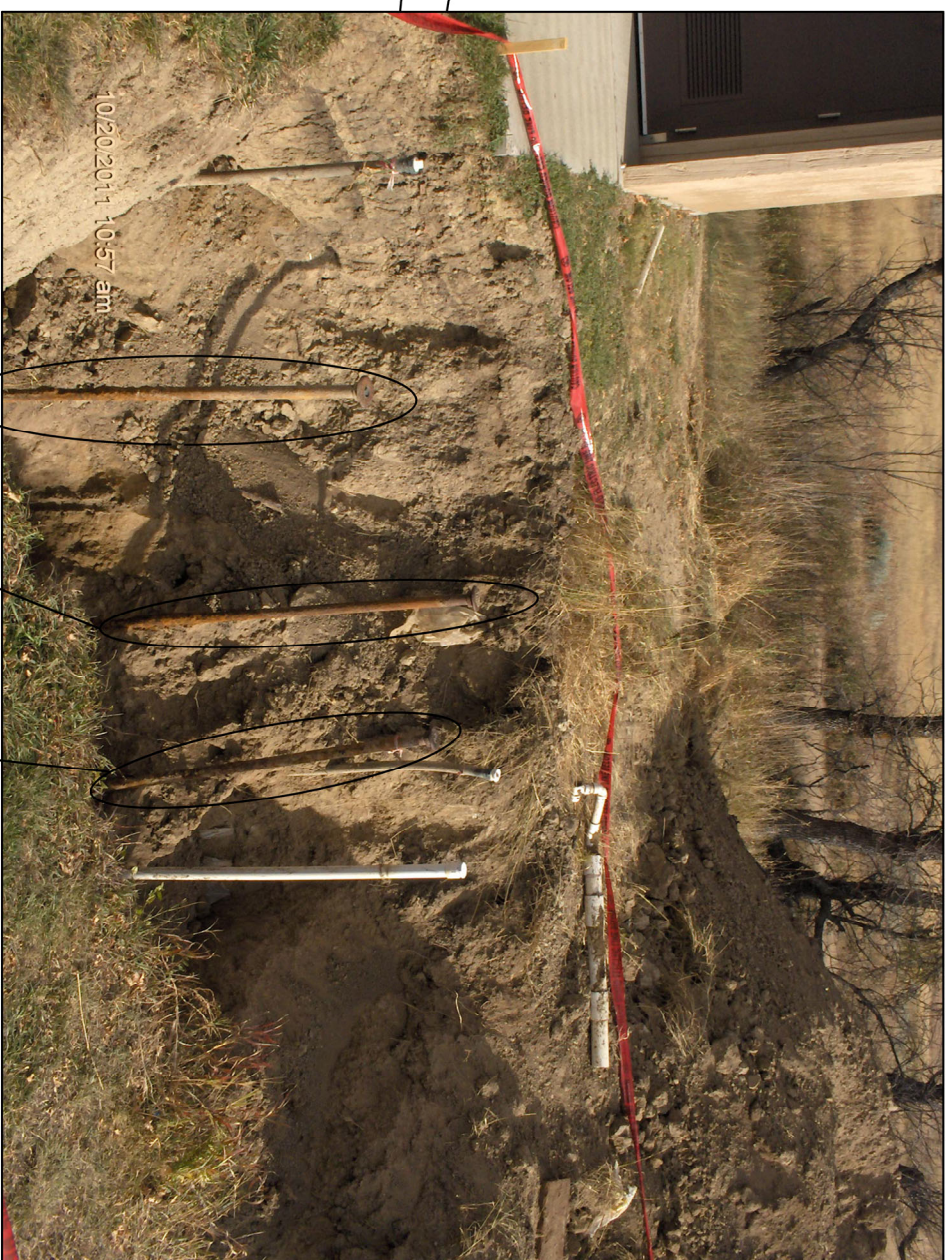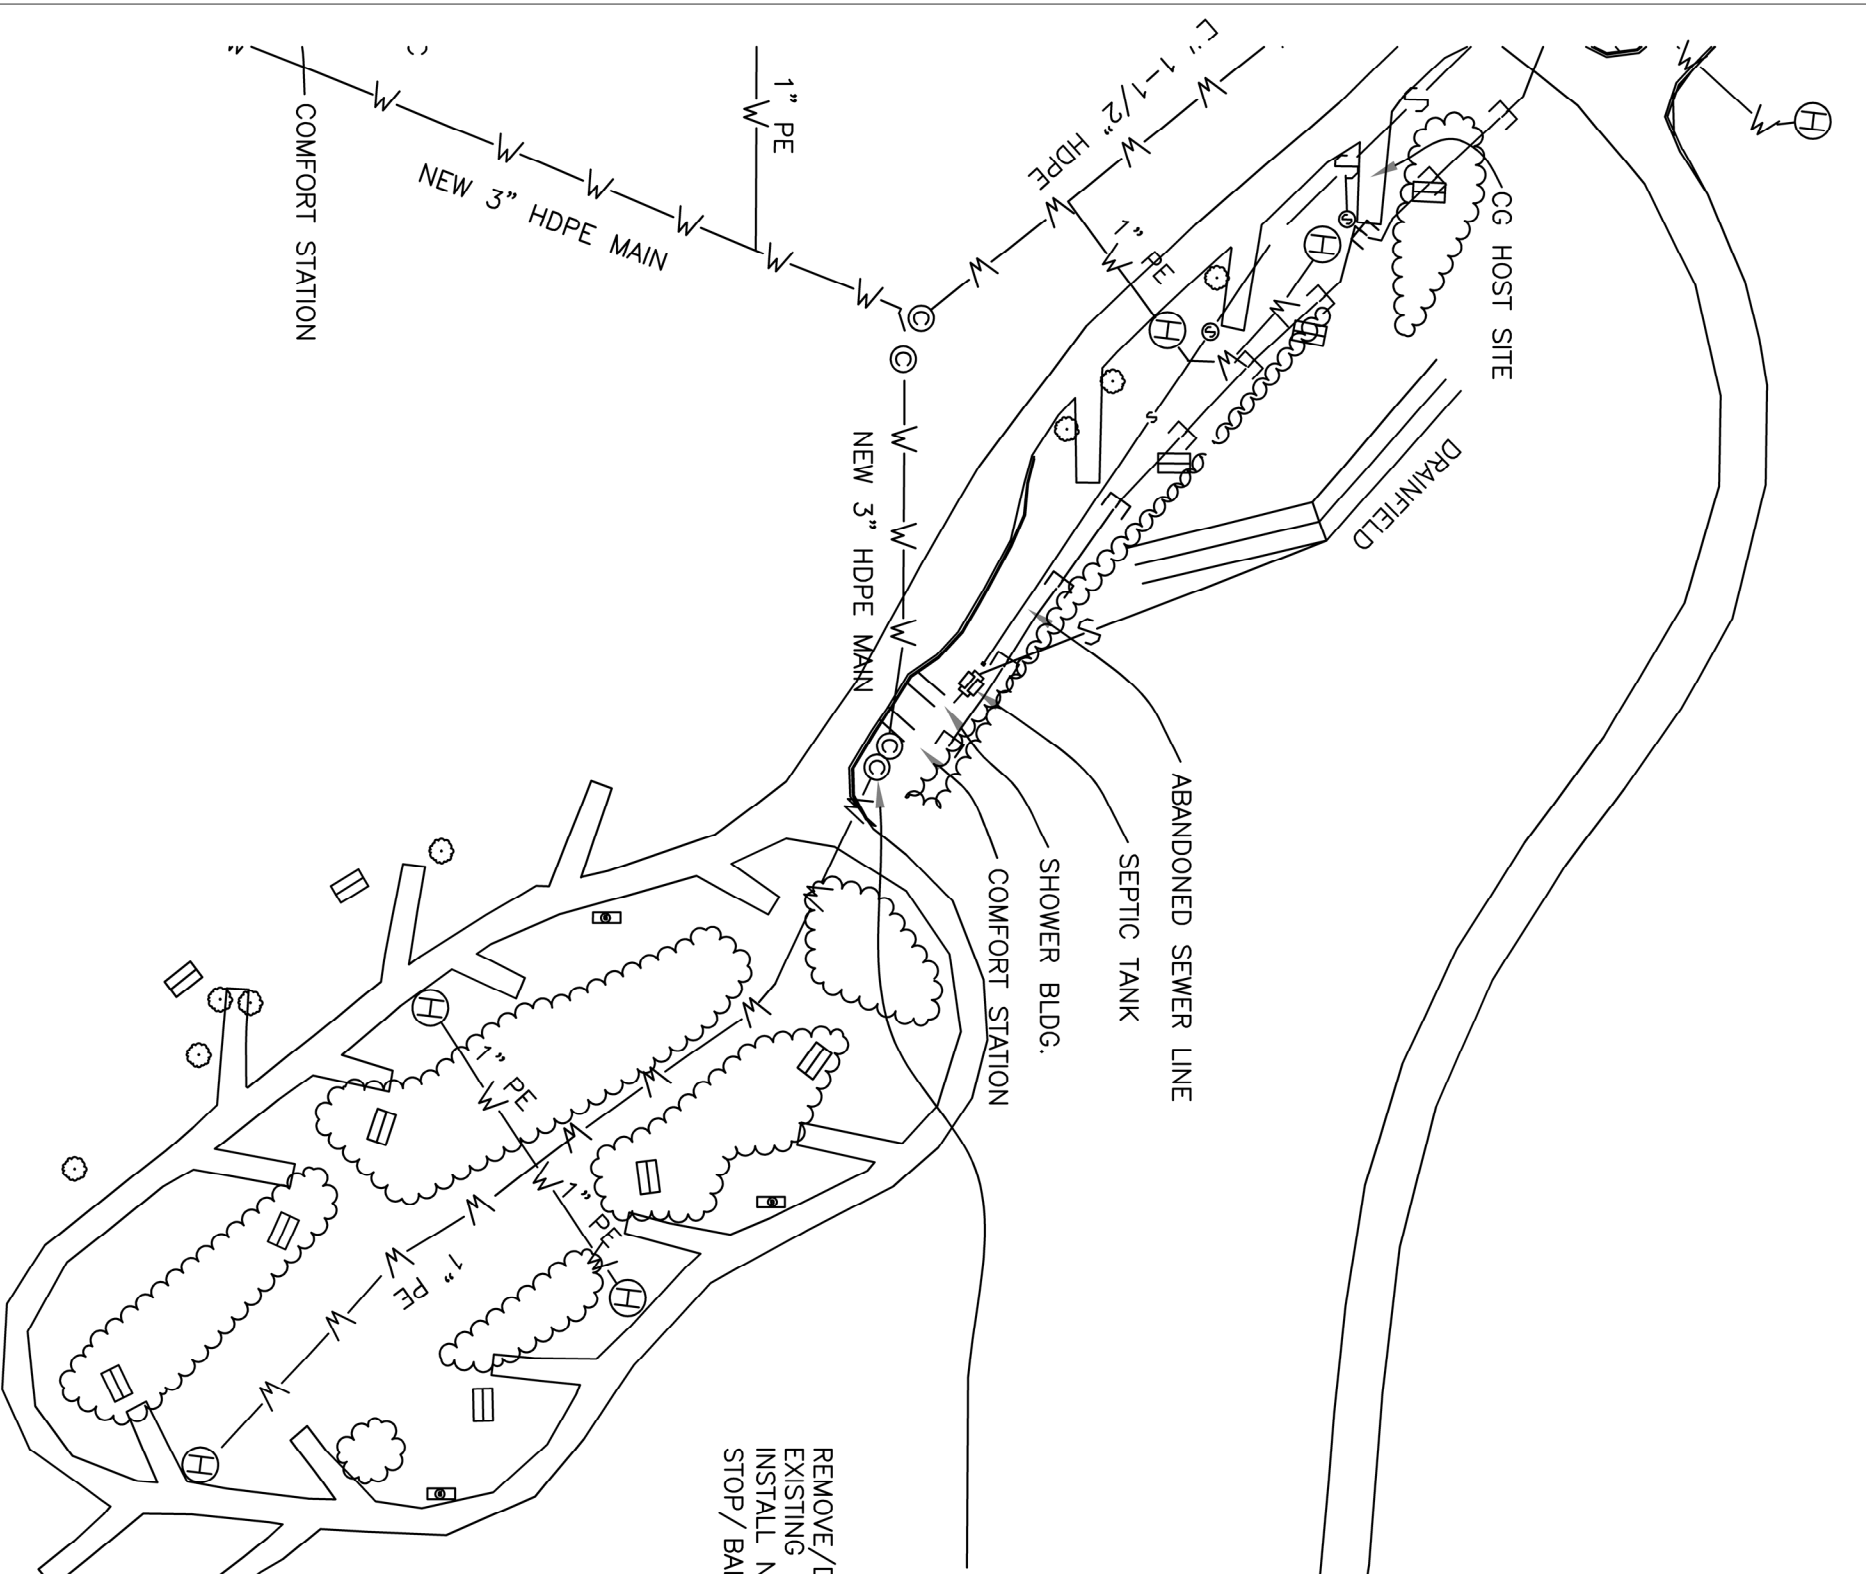

REMOVE/DISPOSE OF THESE
EXISTING CURB STOPS.
INSTALL NEW CURB
STOP/BALL VALVE/PER LINE

CAST IRON EXTENSION TYPE CURB
BOX, MINNEAPOLIS PATTERN. CAST IRON
LID WITH BRASS PENTAGON PLUG.
STATIONARY OPERATING ROD EXTENDING
TO WITHIN 12 IN. OF FINISH GRADE.

CURB STOP WITH PACK JOINTS AS REQUIRED, MINNEAPOLIS TOP THREAD, QUARTER TURN CHECK, STOP & WASTE FEATURE: MUELLER, FORD, OR APPROVED EQUAL (TYP). SIZE CURB STOP VALVE TO REQUIRED WATER LINE SIZE. INSTALL AT STAKED LOCATIONS.

