



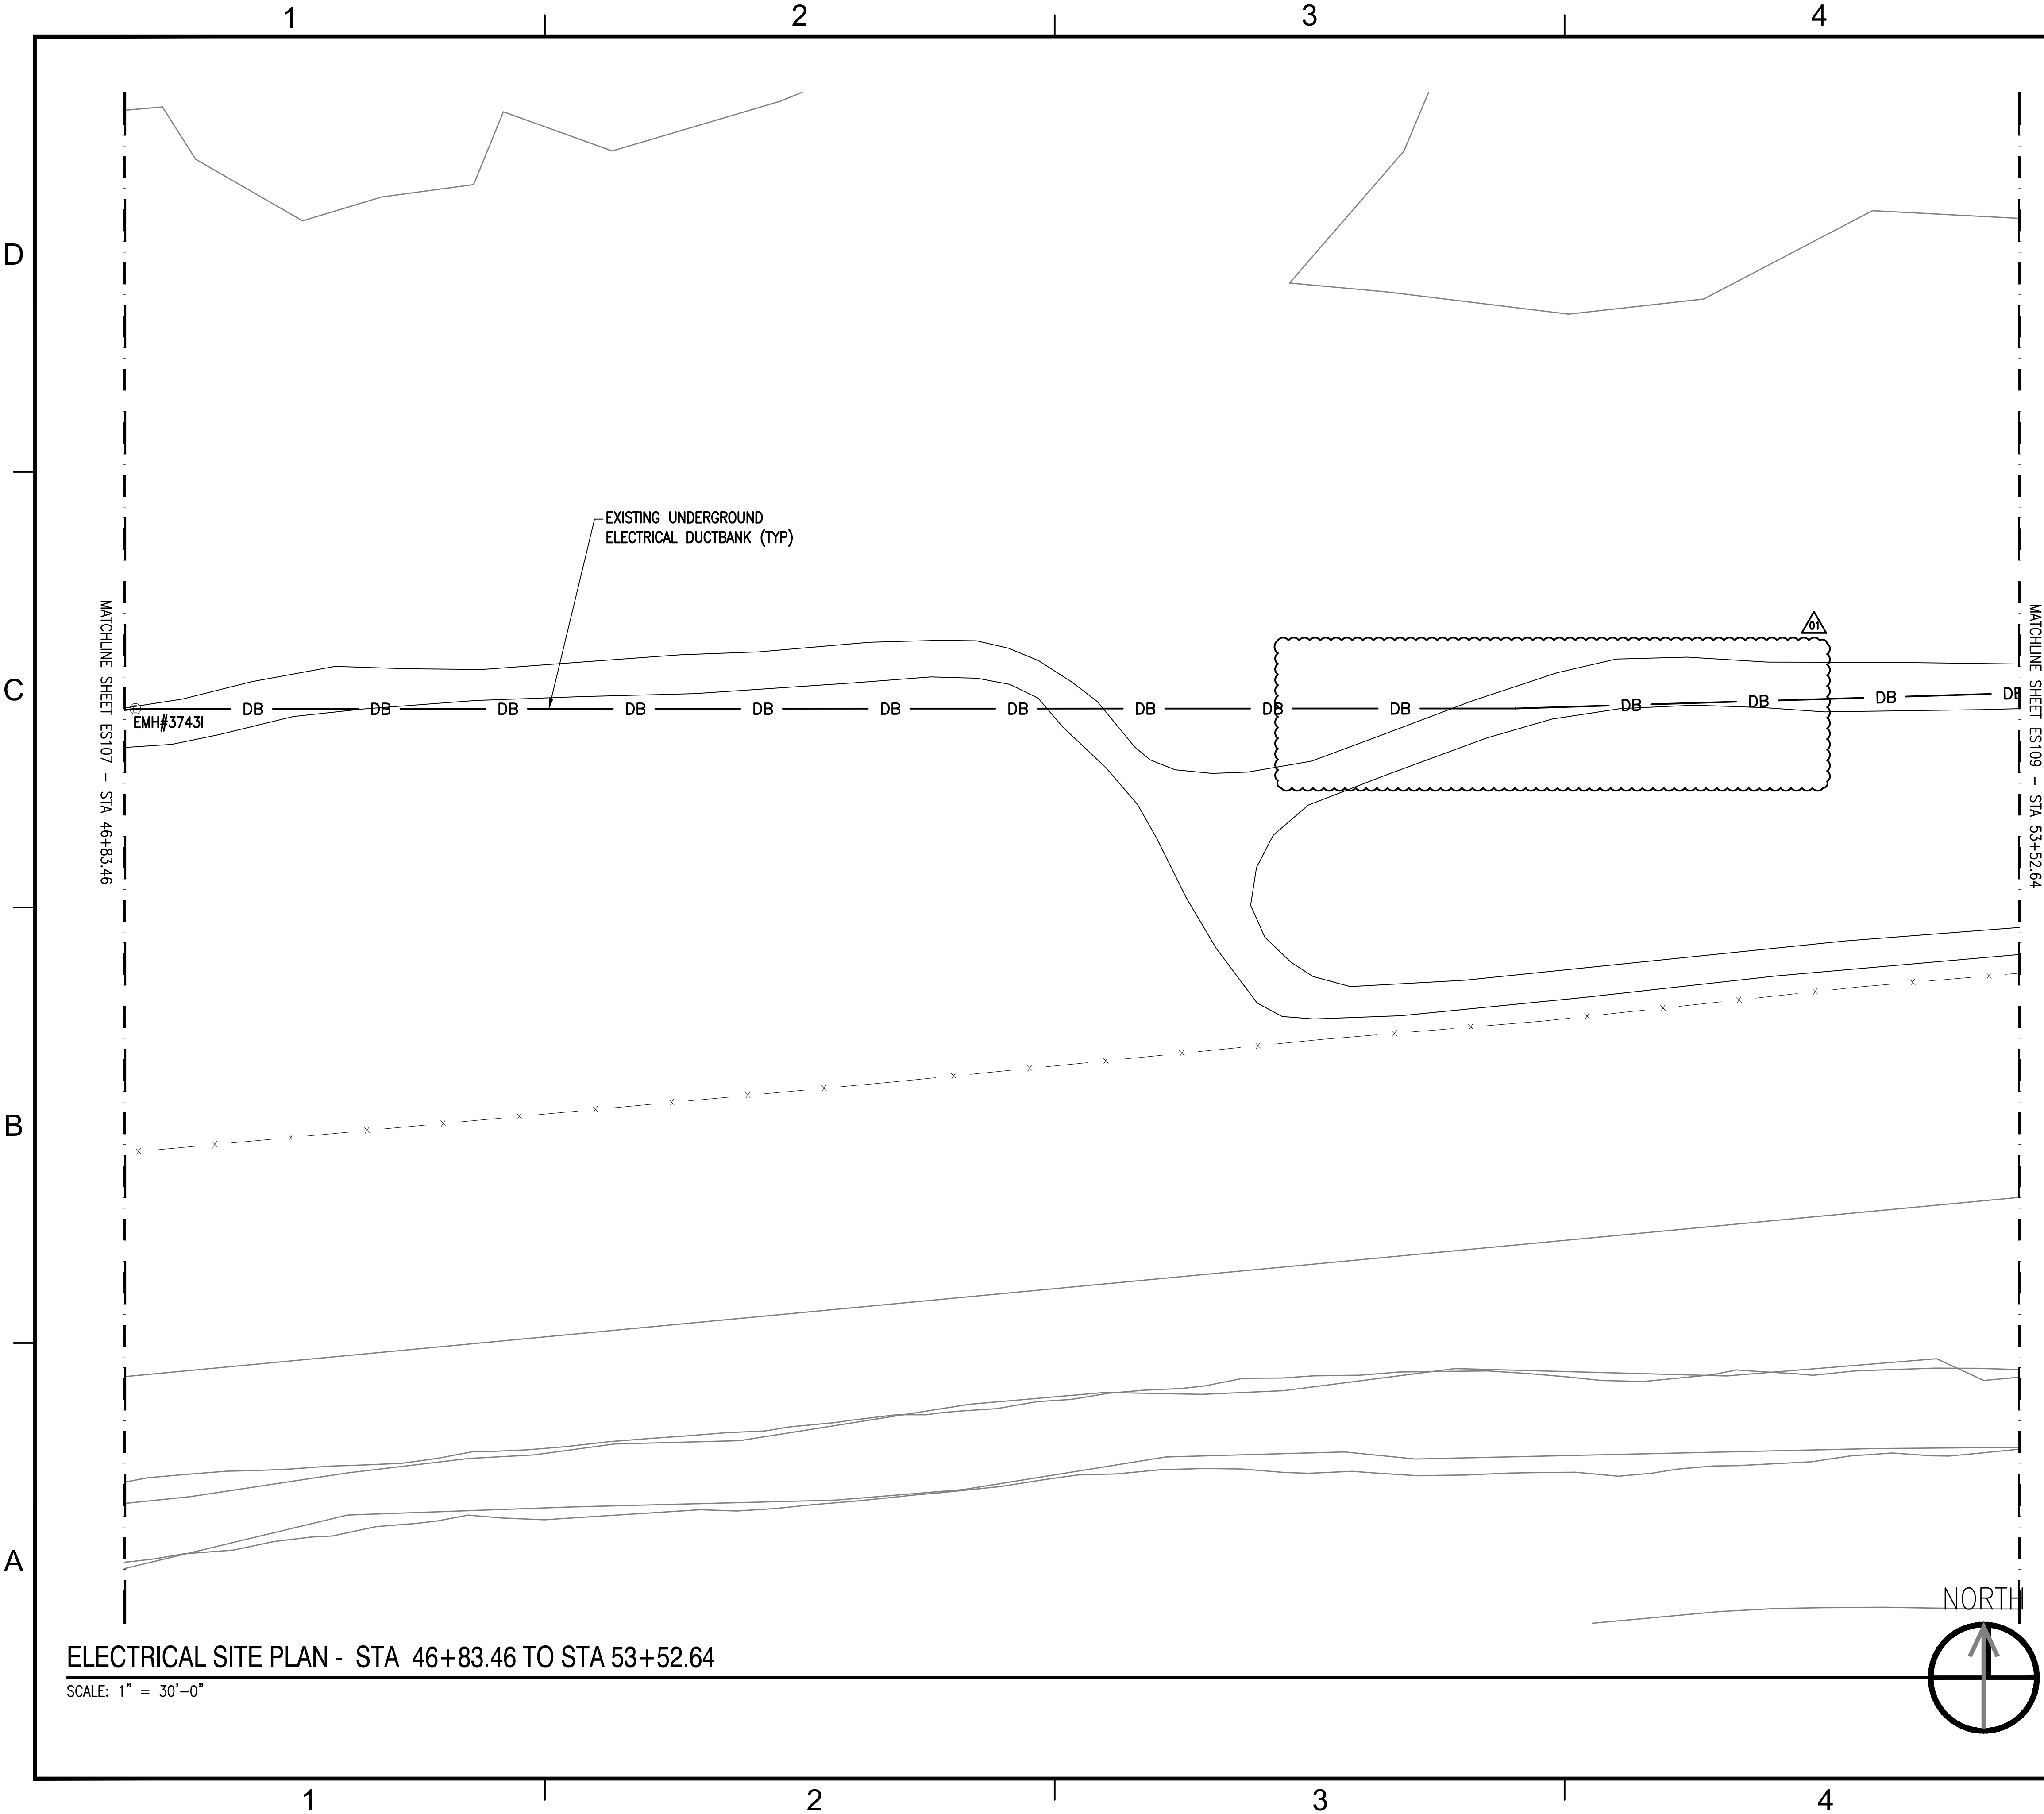

GENERAL SHEET NOTES

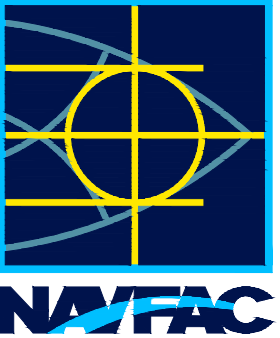

APPROVED

FOR COMMANDER NAVFAC

ACTIVITY

DOUG REYNOLDS, P.E.

SATISFACTORY TO DATE 7/30/25

DES FVP DRW CEV CHK CJM

PMDM CJM

BRANCH MANAGER C. MORTON, P.E.

CHIEF ENGINEER J. MILLER, P.E.

FIRE PROTECTION N/A


NAVFAC

NAVAL FACILITIES ENGINEERING SYSTEMS COMMAND


NAVAL STATION NORFOLK

NORFOLK, VIRGINIA


KEY MAP

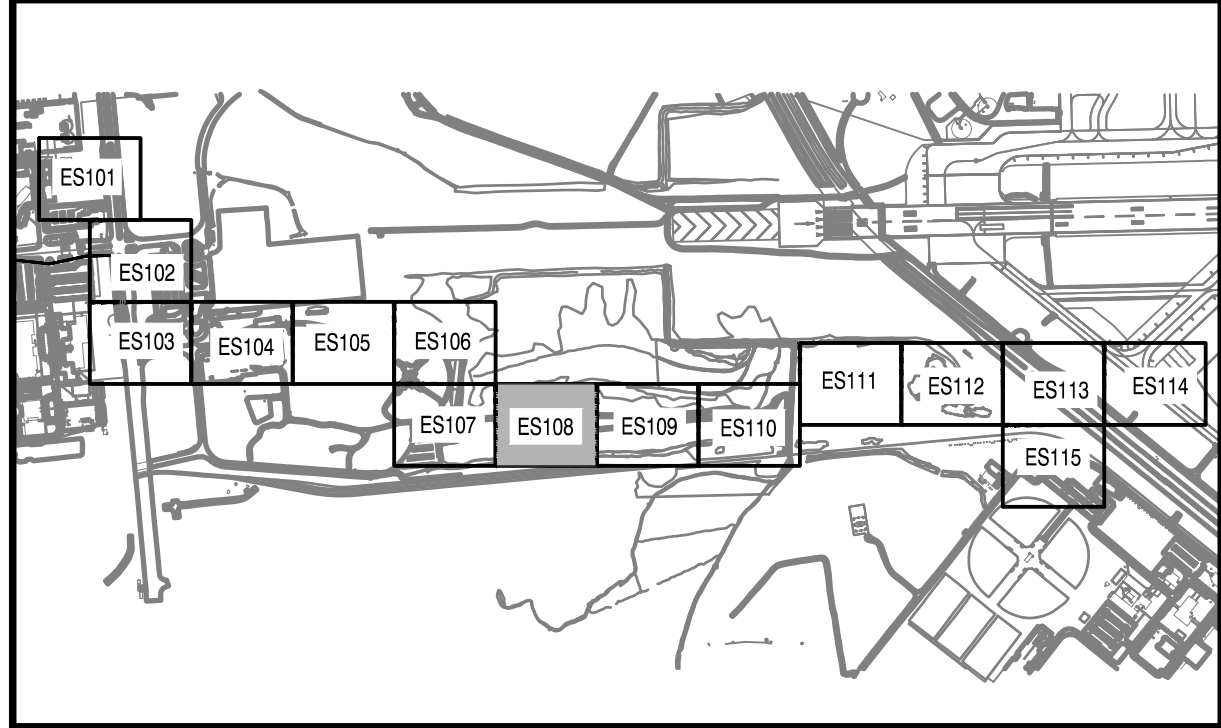



GRAPHIC SCALE

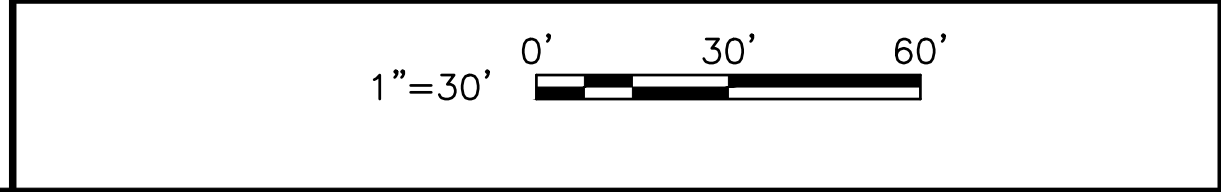

DATE	9/4/25
DESCRIPTION	DESIGN REVISION 01
MARK	01
SEAL	
A/E INFO	
FOR COMMANDER NAVFAC	
ACTIVITY	DOUG REYNOLDS, P.E.
SATISFACTORY TO DATE	7/30/25
DES	FVP
DRW	CEV
CHK	CJM
PMDM	CJM
BRANCH MANAGER	C. MORTON, P.E.
CHIEF ENGINEER	J. MILLER, P.E.
FIRE PROTECTION	N/A
NAVFAC	NAVAL FACILITIES ENGINEERING SYSTEMS COMMAND
NAVAL STATION NORFOLK	NORFOLK, VIRGINIA
NAVAL SUPPORT ACTIVITY	EXTEND 35KV CIRCUIT
ELECTRICAL SITE PLAN	STA 46+83.46 TO STA 53+52.64
SCALE	AS NOTED
PROJECT NO.	1747833
CONSTR. CONTR. NO.	N/A
NAVFAC DRAWING NO.	12927774
SHEET	8 OF 15
ES108	

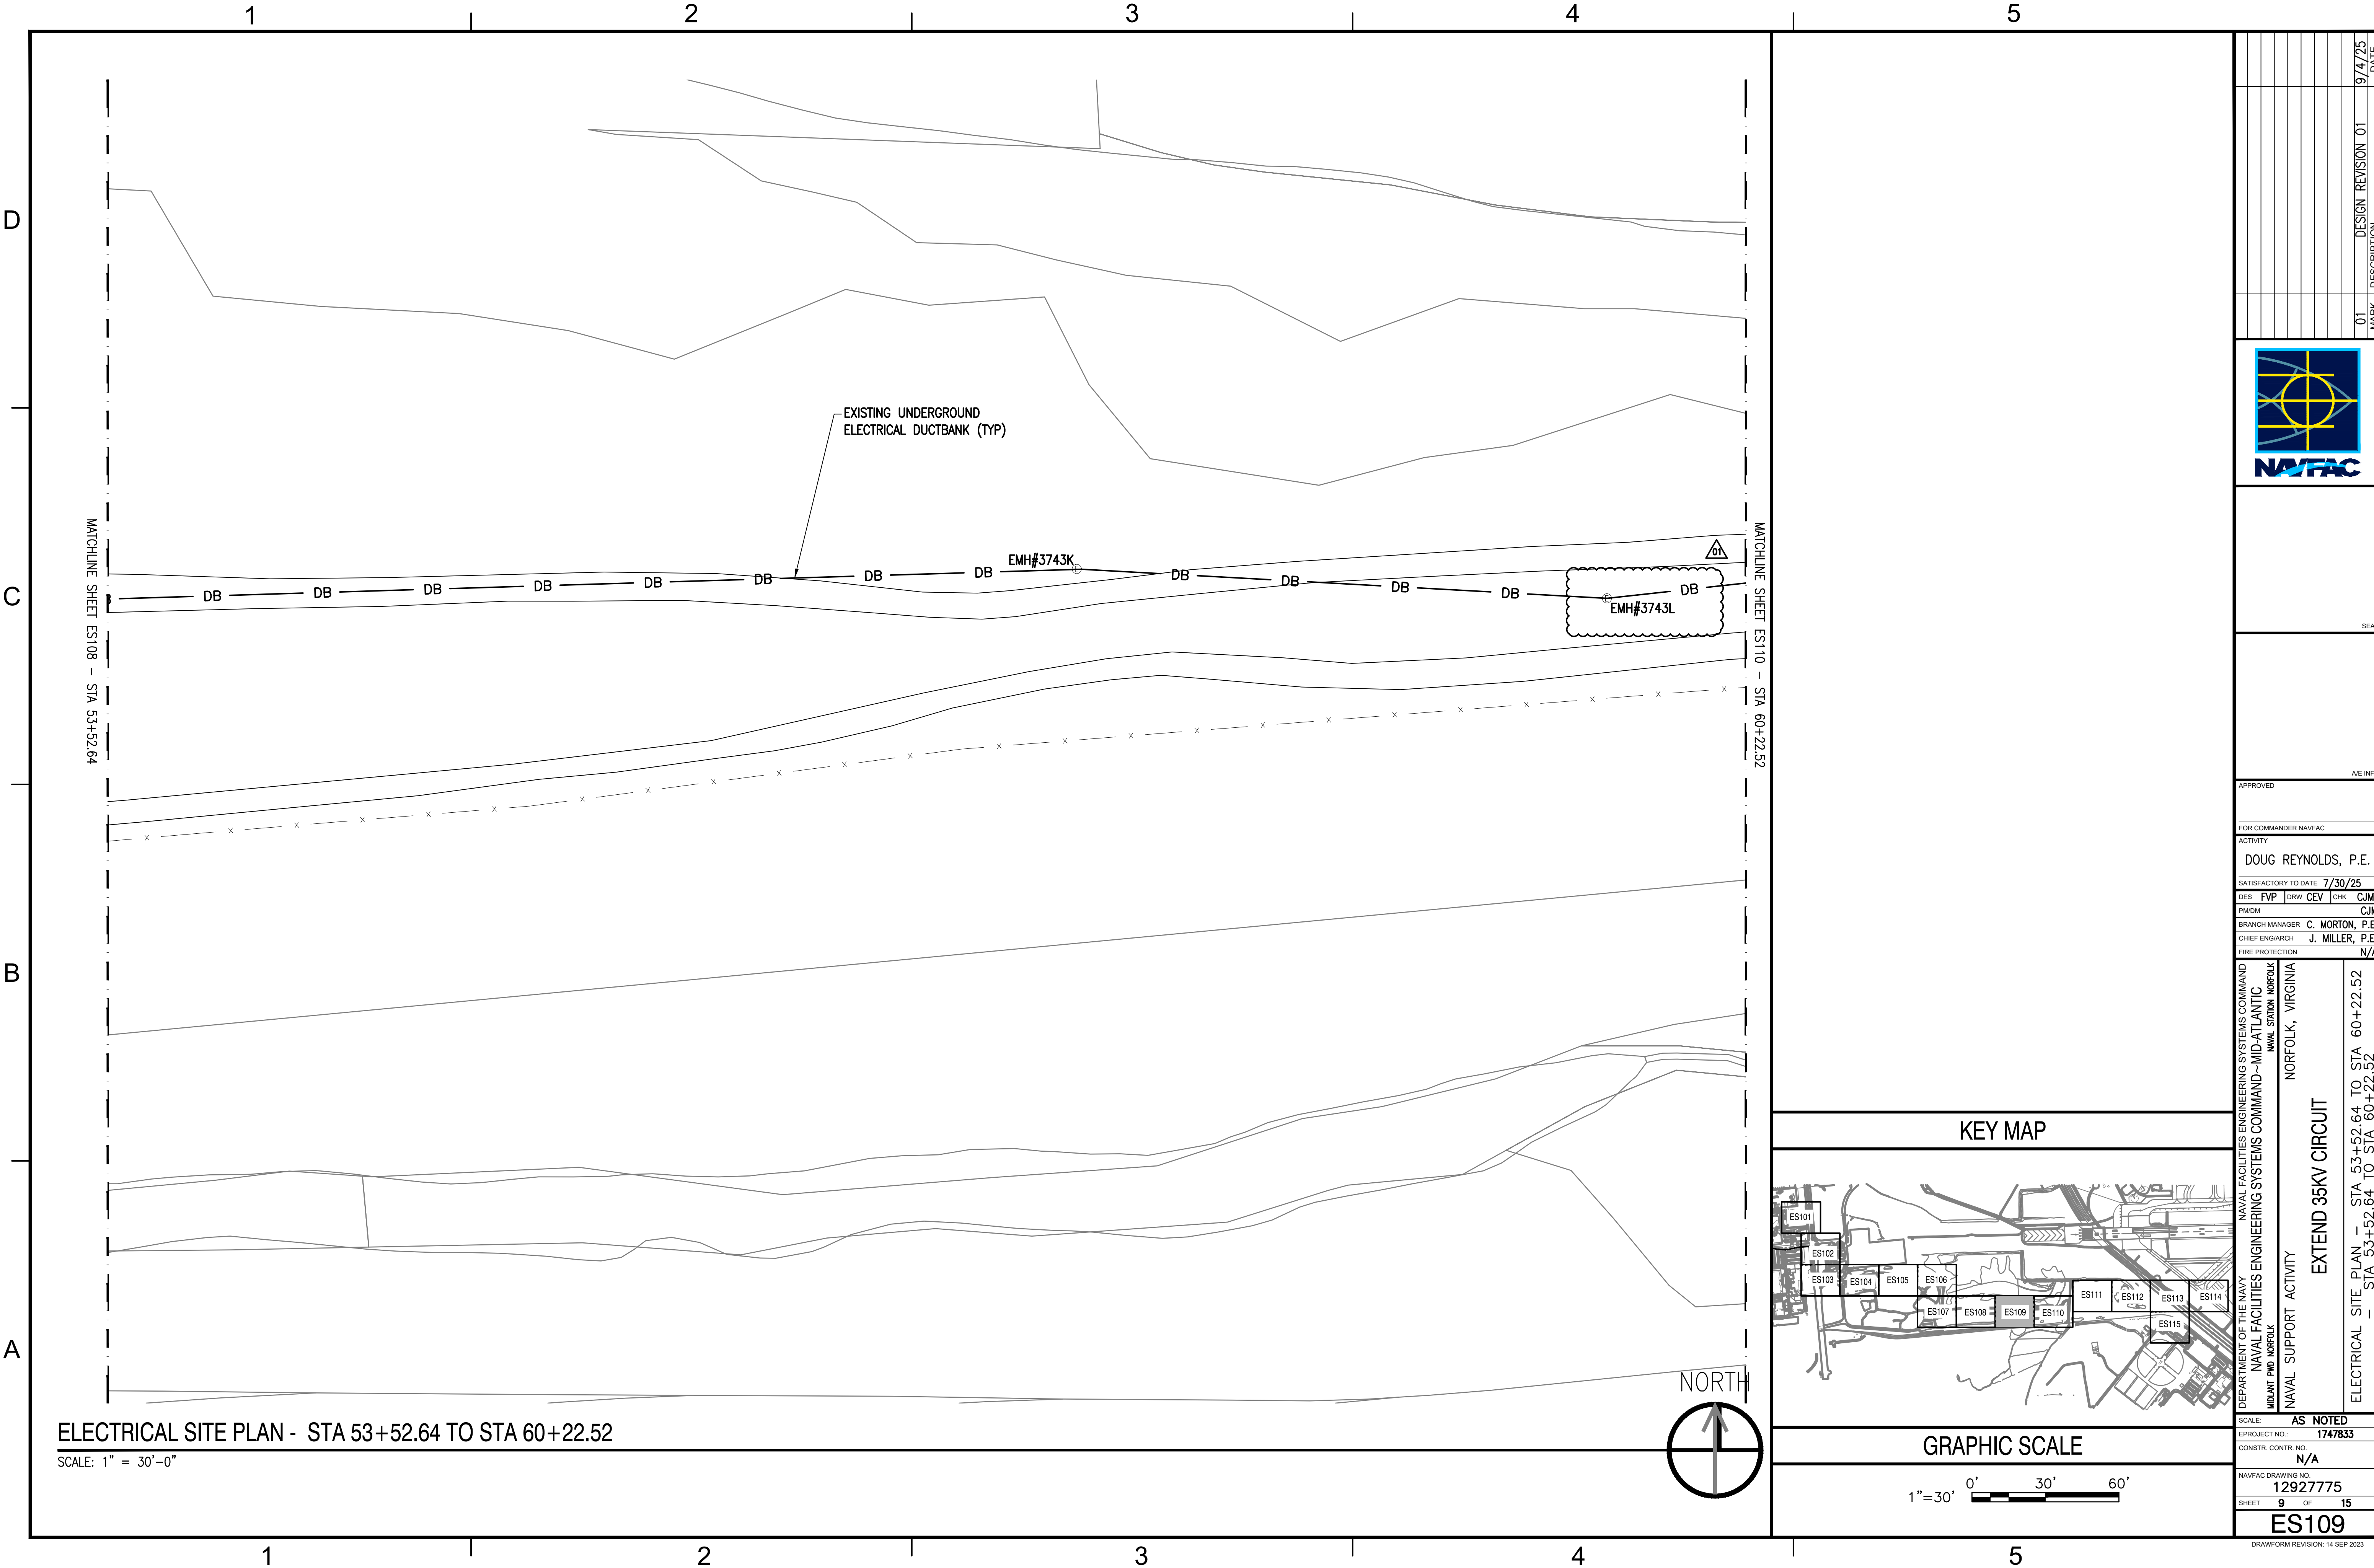

ELECTRICAL SITE PLAN - STA 53+52.64 TO STA 60+22.52
SCALE: 1" = 30'-0"

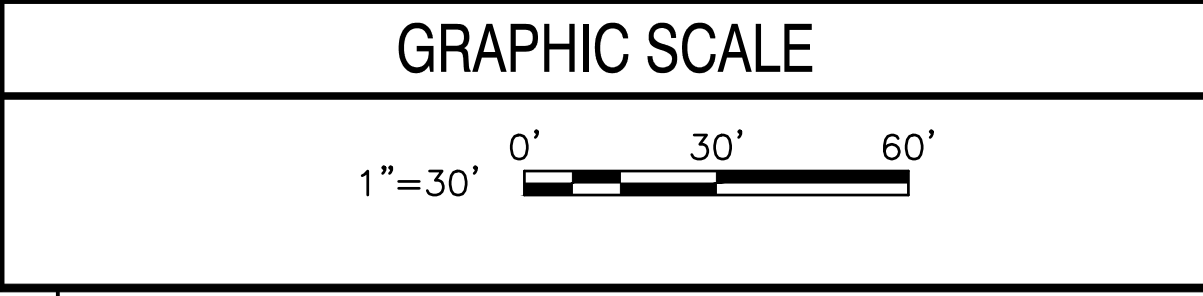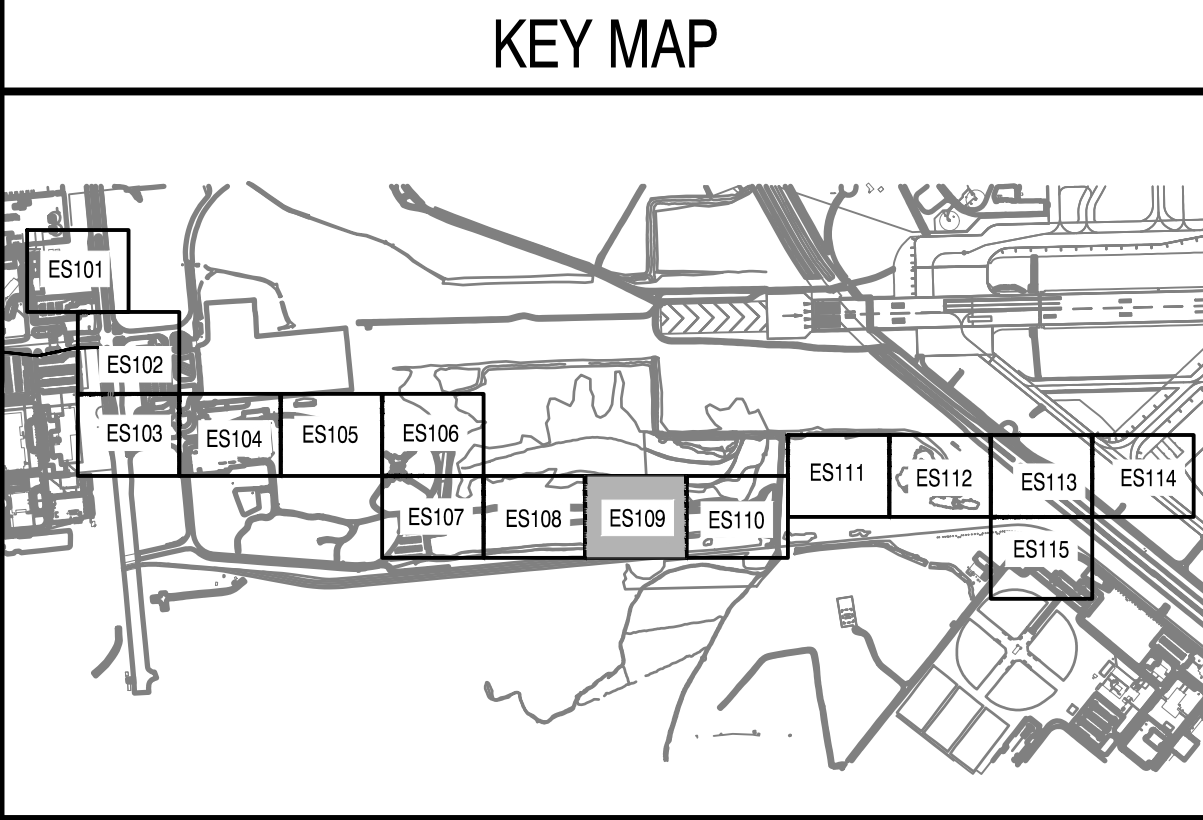

DATE		9/4/25	
DESCRIPTION		DESIGN REVISION 01	
MARK		01	
SEAL			
A/E INFO			
APPROVED			
FOR COMMANDER NAVAC			
ACTIVITY			
DOUG REYNOLDS, P.E.			
SATISFACTORY TO DATE 7/30/25			
DES	FVP	DRW	CEV
CHK	CJM	PMDM	CJM
BRANCH MANAGER	C. MORTON, P.E.	CHIEF ENGINEER	J. MILLER, P.E.
FIRE PROTECTION		N/A	
NAVAL FACILITIES ENGINEERING SYSTEMS COMMAND - MID-ATLANTIC		NORFOLK, VIRGINIA	
NAVAL SUPPORT ACTIVITY		EXTEND 35KV CIRCUIT	
ELECTRICAL SITE PLAN - STA 53+52.64 TO STA 60+22.52		ELECTRICAL SITE PLAN - STA 53+52.64 TO STA 60+22.52	
SCALE: AS NOTED			
PROJECT NO.: 1747833			
CONSTR. CONTR. NO. N/A			
NAVAC DRAWING NO. 12927775			
SHEET 9 OF 15			
ES109			
DRAWING REVISION: 14 SEP 2023			

