

Fort Donelson National Battlefield

Park Identification Sign

June 14, 2007
August 10, 2007 R1
August 21, 2007 R2

0607-514-FODO




Office of NPS Identity
Harpers Ferry Center
Interpretive Design Center
Harpers Ferry, WV 25425
304-535-4069

APPROVAL

Name

Title

Phone

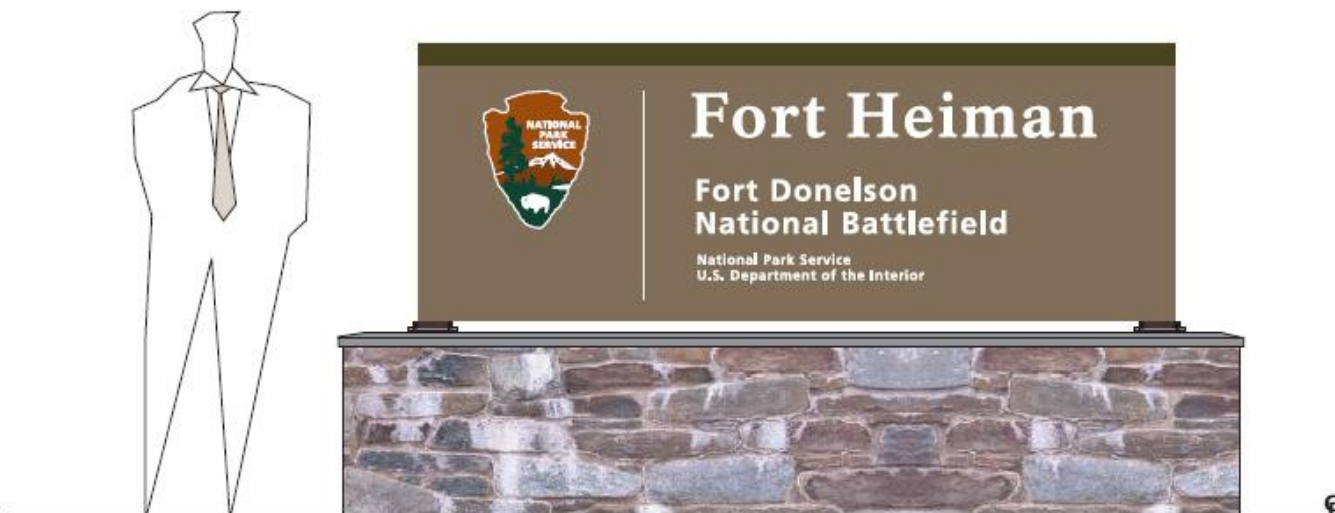

1 - 1.0 Park ID Custom Stone Monolith 2-Sided - Cap Height 6" - 108"x 39 3/4"

PROJECT

**FORT DONELSON
NATIONAL
HISTORICAL SITE**

PROJECT NUMBER

0607-514-FODA

UNIT | AREA

FODA

DRAWING SCALE

1/2" = 1' - 0"

ENLARGE FOR FULL SCALE

2400%

SIGN CATEGORY

Park Identification

DESCRIPTION

STRUCTURE: QTY: 1
Stone Monolith Base

PANEL: QTY: 2
F/Plaf-1GA Per NPS Standards,
2-Sided Western Red Cedar
with routed typography with
full-color arrowhead.

DRAWING DATE

06-14-2007

REVISION | DATE

1	08-10-2007
2	
3	
4	


DRAWING NUMBER

1.0 | FODO



National Park Service
U.S. Department of the Interior
UnitGuide Sign Program
304-635-4069

APPROVAL	
Initials	Date

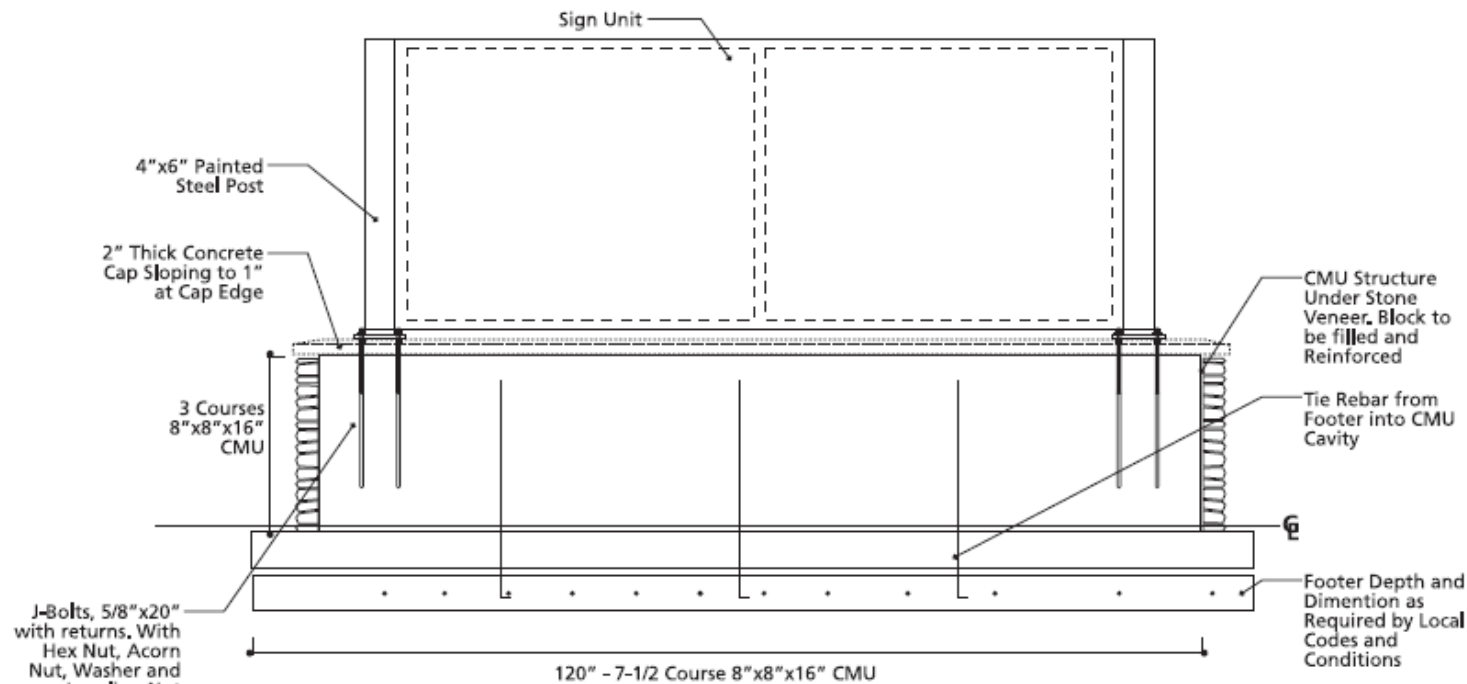

1 - 1.0A Sign Elevation

APPROVAL	
Initials	Date

PROJECT

**FORT DONELSON
NATIONAL
HISTORICAL SITE**

PROJECT NUMBER

0607-514-FODA

UNIT | AREA

FODA

DRAWING SCALE

1/2" = 1' - 0"

ENLARGE FOR FULL SCALE

2400%

SIGN CATEGORY

Park Identification

DESCRIPTION

STRUCTURE: QTY: 1
Stone Monolith Base

PANEL: QTY: 2
F/Plaf-1GA Per NPS Standards,
2-Sided Western Red Cedar
with routed typography with
full-color arrowhead.

DRAWING DATE

06-14-2007

REVISION | DATE


1	08-10-2007
2	
3	
4	

DRAWING NUMBER

1.0A | FODO



National Park Service
U.S. Department of the Interior
UniGuide Sign Program
304-535-4069

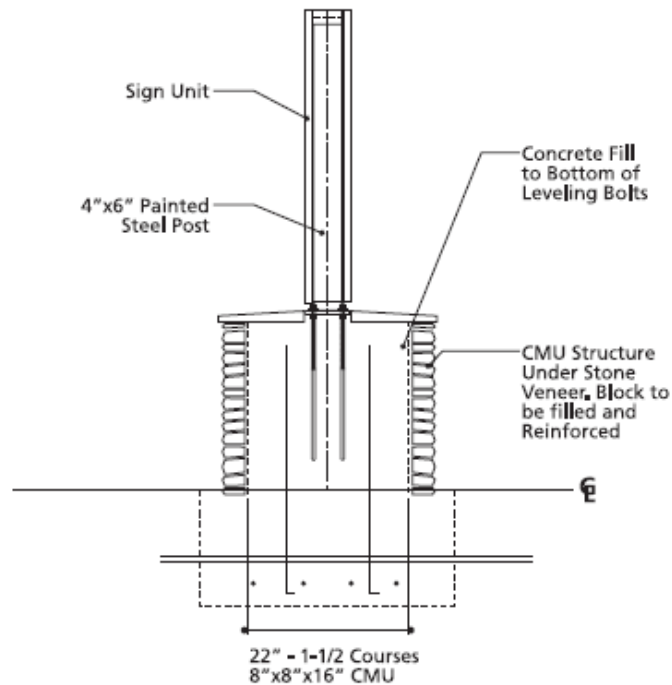

1 - 1.0B Sign Side View

APPROVAL	
Initials	Date

PROJECT

**FORT DONELSON
NATIONAL
HISTORICAL SITE**

PROJECT NUMBER

0607-514-FODA

UNIT | AREA

FODA

DRAWING SCALE

1/2" = 1' - 0"

ENLARGE FOR FULL SCALE

2400%

SIGN CATEGORY

Park Identification

DESCRIPTION

STRUCTURE: QTY: 1
Stone Monolith Base

PANEL: QTY: 1
F/Plaf-1GA Per NPS Standards,
2-Sided Western Red Cedar
with routed typography with
full-color arrowhead.

DRAWING DATE

06-14-2007

REVISION | DATE

1	08-10-2007
2	
3	
4	

DRAWING NUMBER

1.0B | FODO



National Park Service
U.S. Department of the Interior
UniGuide Sign Program
304-635-4069

PROJECT

**FORT DONELSON
NATIONAL
HISTORICAL SITE**

PROJECT NUMBER

0607-514-FODA

UNIT | AREA

FODA

DRAWING SCALE

1/2" = 1' - 0"

ENLARGE FOR FULL SCALE

2400%

SIGN CATEGORY

Park Identification

DESCRIPTION

STRUCTURE: QTY: 1
Stone Monolith Base

PANEL: QTY: 2

F/Plaf-1GA Per NPS Standards,
2-Sided Western Red Cedar
with routed typography with
full-color arrowhead.

DRAWING DATE

06-14-2007

REVISION | DATE


1	08-10-2007
2	
3	
4	

DRAWING NUMBER

1.0C | FODO



National Park Service
U.S. Department of the Interior
UniGuide Sign Program
304-535-4069

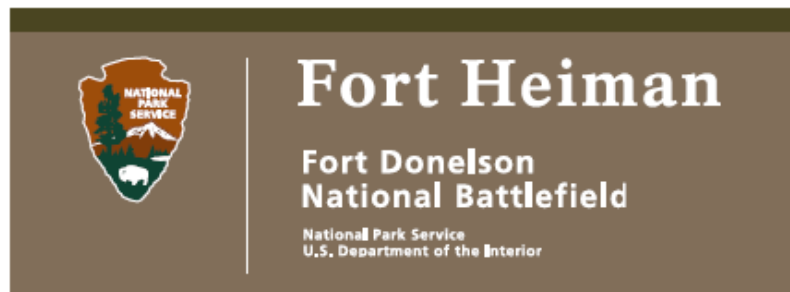


1 - 1.0C Sign Panel, Front and Back - Cap Height 6" - 108"x 39 3/4"

1

APPROVAL

Initials

Date

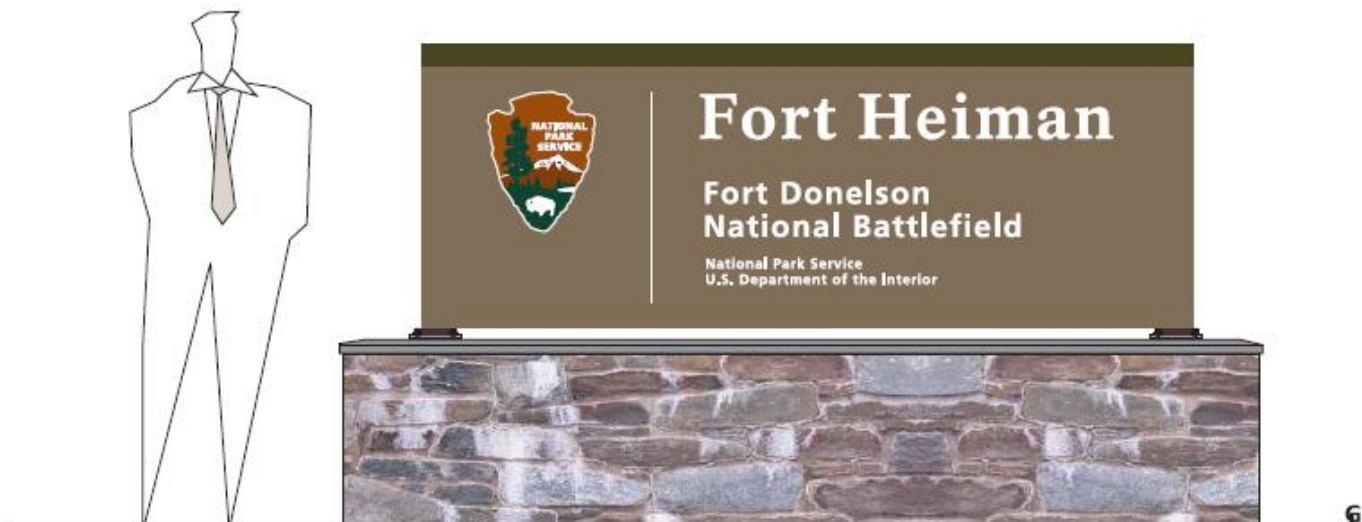

1 - 2.0 Park ID Custom Stone Monolith 2-Sided - Cap Height 6" - 108"x 39 3/4"

1

APPROVAL	
Initials	Date

PROJECT	
FORT DONELSON NATIONAL HISTORICAL SITE	
PROJECT NUMBER	
0607-514-FODA	
UNIT AREA	
FODA	
DRAWING SCALE	
1/2" = 1' - 0"	
ENLARGE FOR FULL SCALE	
2400%	
SIGN CATEGORY	
Park Identification	
DESCRIPTION	
STRUCTURE:	QTY: 1
Stone Monolith Base	
PANEL:	QTY: 1
F/Plaf-1GA Per NPS Standards, Western Red Cedar with routed typography and blank NPS Brown MP07458 back panel with full-color arrowhead.	
DRAWING DATE	
06-14-2007	
REVISION DATE	
1	08-10-2007
2	
3	
4	
DRAWING NUMBER	
2.0 FODO	



National Park Service
U.S. Department of the Interior
UnitGuide Sign Program
304-535-4069

**FORT DONELSON
NATIONAL
HISTORICAL SITE**

PROJECT NUMBER

0607-514-FODA

UNIT | AREA

FODA

DRAWING SCALE

1/2" = 1' - 0"

ENLARGE FOR FULL SCALE

2400%

SIGN CATEGORY

Park Identification

DESCRIPTION

STRUCTURE: QTY: 1
Stone Monolith Base

PANEL: QTY: 1
F/Plaf-1GA Per NPS Standards,
Western Red Cedar with
routed typography and blank
NPS Brown MP07458 back
panel with full-color
arrowhead.

DRAWING DATE

06-14-2007

REVISION | DATE

1	08-10-2007
---	------------

2	
---	--

3	
---	--


4	
---	--

DRAWING NUMBER

2.0A | FODO



National Park Service
U.S. Department of the Interior
UniGuide Sign Program
304-635-4069

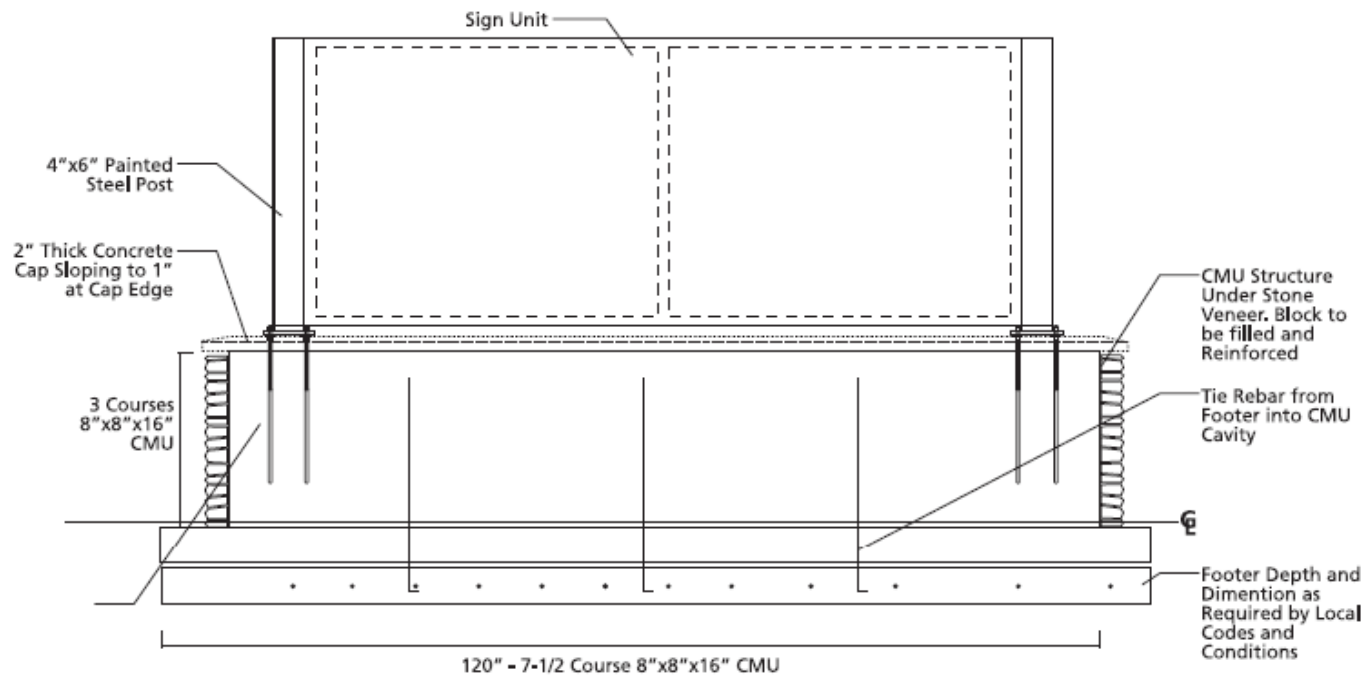


1 - 2.0A Sign Elevation

APPROVAL

Initials

Date

1

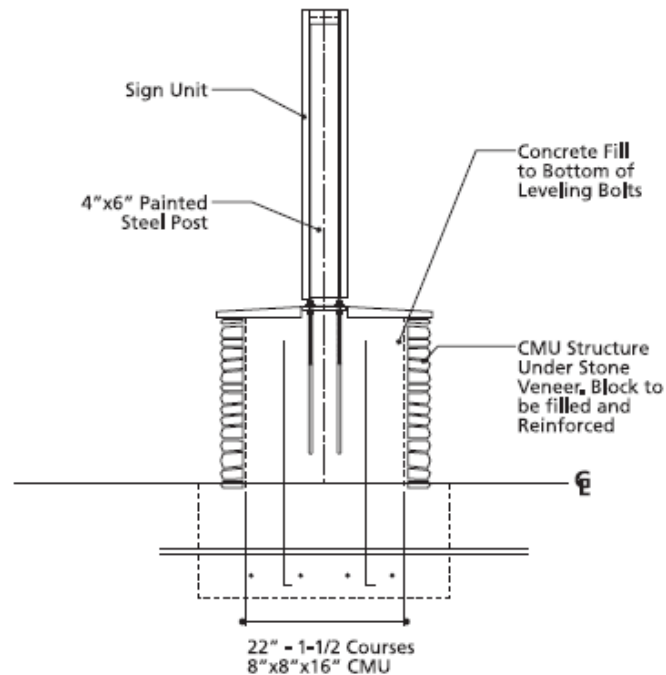

1 - 2.0B Sign Side View

APPROVAL	
Initials	Date

PROJECT

**FORT DONELSON
NATIONAL
HISTORICAL SITE**

PROJECT NUMBER

0607-514-FODA

UNIT | AREA

FODA

DRAWING SCALE

1/2" = 1' - 0"

ENLARGE FOR FULL SCALE

2400%

SIGN CATEGORY

Park Identification

DESCRIPTION

STRUCTURE: QTY: 1
Stone Monolith Base

PANEL: QTY: 1
F/Plaf-1GA Per NPS Standards,
Western Red Cedar with
routed typography and blank
NPS Brown MP07458 back
panel with full-color
arrowhead.

DRAWING DATE

06-14-2007

REVISION | DATE


1	08-10-2007
2	
3	
4	

DRAWING NUMBER

2.0B | FODO



National Park Service
U.S. Department of the Interior
UniGuide Sign Program
304-635-4069

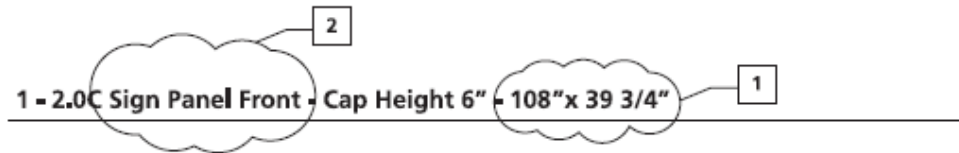

APPROVAL	
Initials	Date

PROJECT

**FORT DONELSON
NATIONAL
HISTORICAL SITE**

PROJECT NUMBER

0607-514-FODA

UNIT | AREA

FODA

DRAWING SCALE

1/2" = 1' - 0"

ENLARGE FOR FULL SCALE

2400%

SIGN CATEGORY

Park Identification

DESCRIPTION

STRUCTURE: QTY: 1
Stone Monolith Base

PANEL: QTY: 1

F/Plaf-1GA Per NPS Standards, Western Red Cedar with routed typography and blank NPS Brown MP07458 back panel with full-color arrowhead.

DRAWING DATE

06-14-2007

REVISION | DATE

1	08-10-2007
2	08-21-2007
3	
4	

DRAWING NUMBER

2.0C | FODO



National Park Service
U.S. Department of the Interior
UniGuide Sign Program
304-635-4069



1 - 2.0D Sign Back Panel

APPROVAL	
_____ Initials	_____ Date

PROJECT	
FORT DONELSON NATIONAL HISTORICAL SITE	
PROJECT NUMBER	
0607-514-FODA	
UNIT AREA	
FODA	
DRAWING SCALE	
1/2" = 1' - 0"	
ENLARGE FOR FULL SCALE	
2400%	
SIGN CATEGORY	
Park Identification	
DESCRIPTION	
STRUCTURE: QTY: 1 Stone Monolith Base	
PANEL: QTY: 1 F/Plaf-1GA Per NPS Standards, Western Red Cedar with routed typography and blank NPS Brown MP07458 back panel with full-color arrowhead.	
DRAWING DATE	
06-14-2007	
REVISION DATE	
1	08-10-2007
2	
3	
4	
DRAWING NUMBER	
2.0D FODO	

Fort Donelson National Historic Site


Facility Identity Signs

August 8, 2008

0808-727-FODO



Office of NPS Identity
Harpers Ferry Center
Interpretive Design Center
Harpers Ferry, WV 25425
304-535-4069

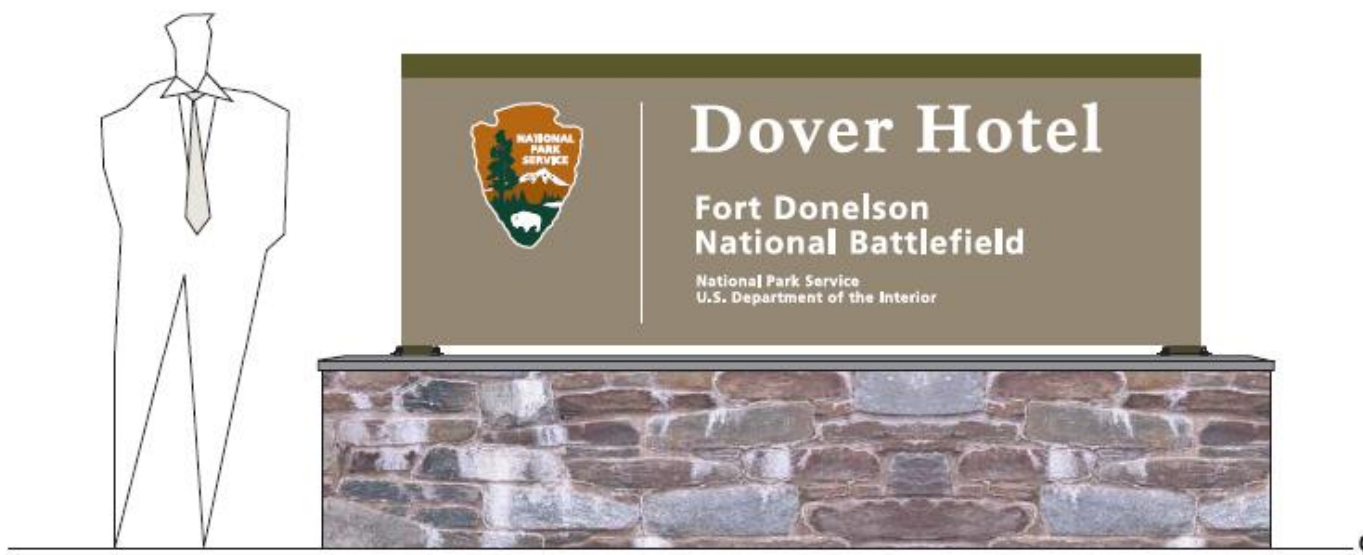

1 - 1.0 Custom Stone Monolith 1-Sided Park ID Sign
 Cap Height 6" - 108" x 39 3/4"

PROJECT

**FORT DONELSON
 NATIONAL
 HISTORIC SITE**

**PROJECT NUMBER
 0808-727-FODO**

UNIT | AREA

Dover Hotel

DRAWING SCALE

1/2" = 1' - 0"

**ENLARGE FOR FULL SCALE
 2400%**

SIGN CATEGORY

Identification

DESCRIPTION

STRUCTURE: QTY:
 Stone Monolith Base, To Be
 Provided By Park

PANEL: QTY: 1
 F/Plaf-1GA Per NPS Standards,
 1-Sided Western Red Cedar
 with Blank Back, Routed
 Typography and Full-color
 Arrowhead, Per NPS Standards

DRAWING DATE

08-08-2008

REVISION | DATE


1	
2	
3	
4	

DRAWING NUMBER

1.0 | FODO



National Park Service
 U.S. Department of the Interior
 UniGuide Sign Program
 306-535-6059

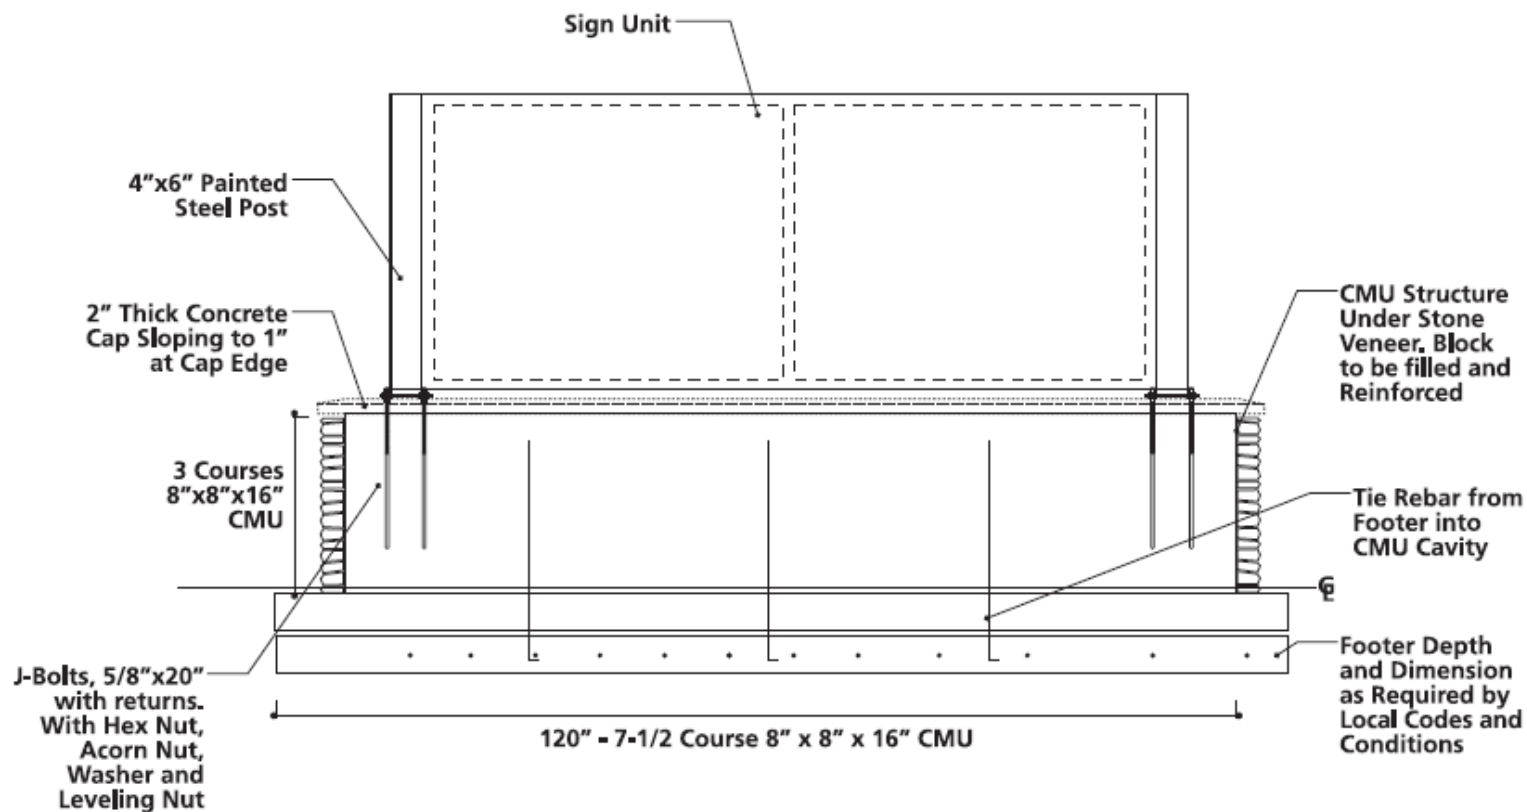

PROJECT

**FORT DONELSON
NATIONAL
HISTORIC SITE**

PROJECT NUMBER

0808-727-FODO

UNIT | AREA

Dover Hotel

DRAWING SCALE

1/2" = 1' - 0"

ENLARGE FOR FULL SCALE

2400%

SIGN CATEGORY

Identification

DESCRIPTION

STRUCTURE: QTY: 1
Stone Monolith Base, To Be Provided By Park

PANEL: QTY: 1
F/Plaf-1GA Per NPS Standards, 1-Sided Western Red Cedar with Blank Back, Routed Typography and Full-color Arrowhead, Per NPS Standards

DRAWING DATE

08-08-2008

REVISION | DATE

1

2

3


4

DRAWING NUMBER

1.0A | FODO



National Park Service
U.S. Department of the Interior
UniGuide Sign Program
304-635-4069

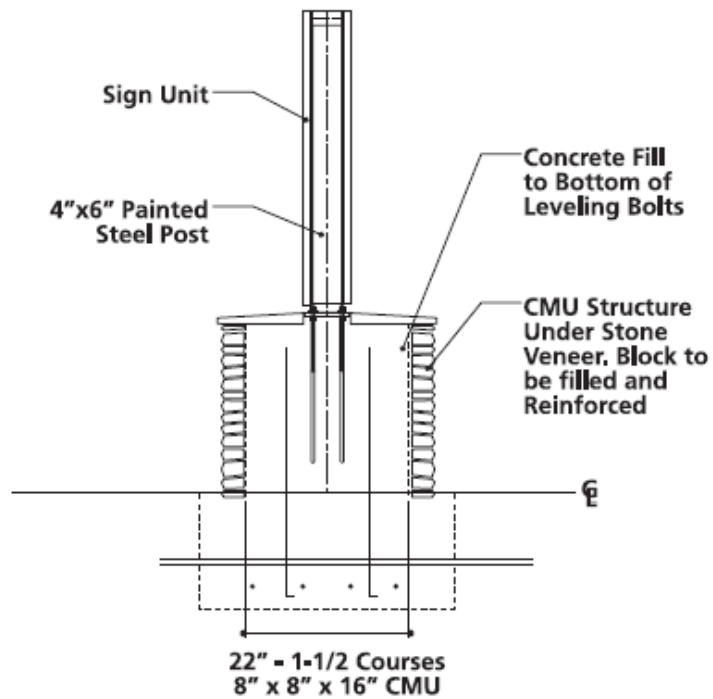

1 - 1.0B Sign Side Elevation

PROJECT

**FORT DONELSON
NATIONAL
HISTORIC SITE**

PROJECT NUMBER

0808-727-FODO

UNIT | AREA

Dover Hotel

DRAWING SCALE

1/2" = 1' - 0"

ENLARGE FOR FULL SCALE

2400%

SIGN CATEGORY

Identification

DESCRIPTION

STRUCTURE: QTY: 1
Stone Monolith Base, To Be
Provided By Park

PANEL: QTY: 1
F/Plaf-1GA Per NPS Standards,
1-Sided Western Red Cedar
with Blank Back, Routed
Typography and Full-color
Arrowhead, Per NPS Standards

DRAWING DATE

08-08-2008

REVISION | DATE

1

2

3


4

DRAWING NUMBER

1.0B | FODO



National Park Service
U.S. Department of the Interior
Interpretive Sign Program
304-635-4069

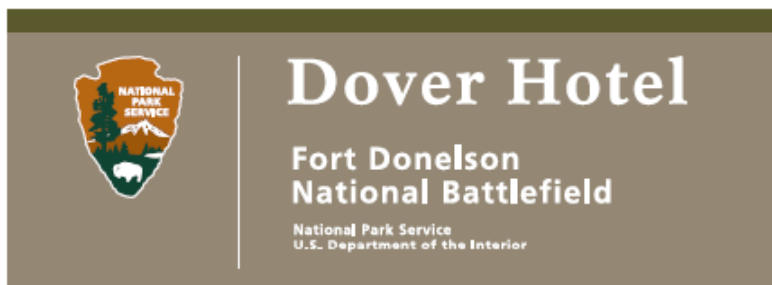

1 - 1.0C Front Sign Panel

Cap Height 6" - 108" x 39 3/4"

PROJECT

**FORT DONELSON
NATIONAL
HISTORIC SITE**

PROJECT NUMBER

0808-727-FODO

UNIT | AREA

Dover Hotel

DRAWING SCALE

1/2" = 1' - 0"

ENLARGE FOR FULL SCALE

2400%

SIGN CATEGORY

Identification

DESCRIPTION

STRUCTURE: QTY:
Stone Monolith Base, To Be
Provided By Park

PANEL: QTY: 1
F/Plaf-1GA Per NPS Standards,
1-Sided Western Red Cedar
with Blank Back, Routed
Typography and Full-color
Arrowhead, Per NPS Standards

DRAWING DATE

08-08-2008

REVISION | DATE

1	
2	
3	
4	

DRAWING NUMBER

1.0C | FODO



National Park Service
U.S. Department of the Interior
UniGuide Sign Program
304-535-4059



1 - 1.0D Back Sign Panel

108" x 39 3/4"

PROJECT
FORT DONELSON
NATIONAL
HISTORIC SITE
PROJECT NUMBER
0808-727-FODO

UNIT | AREA
Dover Hotel
DRAWING SCALE
1/2" = 1' - 0"
ENLARGE FOR FULL SCALE
2400%

SIGN CATEGORY
Identification


DESCRIPTION
STRUCTURE: QTY:
Stone Monolith Base, To Be
Provided By Park

PANEL: QTY: 1
F/Plaf-1GA Per NPS Standards,
1-Sided Western Red Cedar
with Blank Back, Routed
Typography and Full-color
Arrowhead, Per NPS Standards

DRAWING DATE
08-08-2008

REVISION DATE	
1	
2	
3	
4	

DRAWING NUMBER
1.0D | FODO

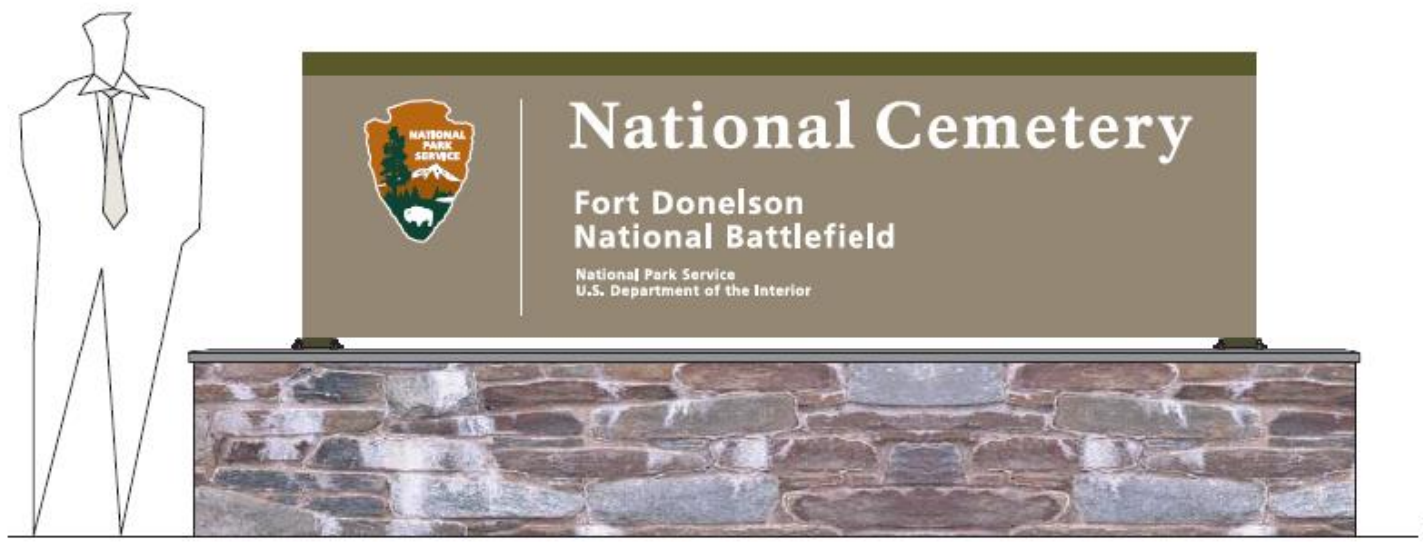

1 - 2.0 Custom Stone Monolith 1-Sided Park ID Sign

Cap Height 6" - 132" x 39 3/4"

PROJECT

**FORT DONELSON
NATIONAL
HISTORIC SITE**

PROJECT NUMBER

0808-727-FODO

UNIT | AREA

Dover Hotel

DRAWING SCALE

1/2" = 1' - 0"

ENLARGE FOR FULL SCALE

2400%

SIGN CATEGORY

Identification

DESCRIPTION

STRUCTURE: QTY:
Stone Monolith Base, To Be
Provided By Park

PANEL: QTY: 1
F/Plaf-1GA Per NPS Standards,
1-Sided Western Red Cedar
with Blank Back, Routed
Typography and Full-color
Arrowhead, Per NPS Standards

DRAWING DATE

08-08-2008

REVISION | DATE

1

2

3


4

DRAWING NUMBER

2.0 | FODO



National Park Service
U.S. Department of the Interior
UnitGuide Sign Program
304-635-6089

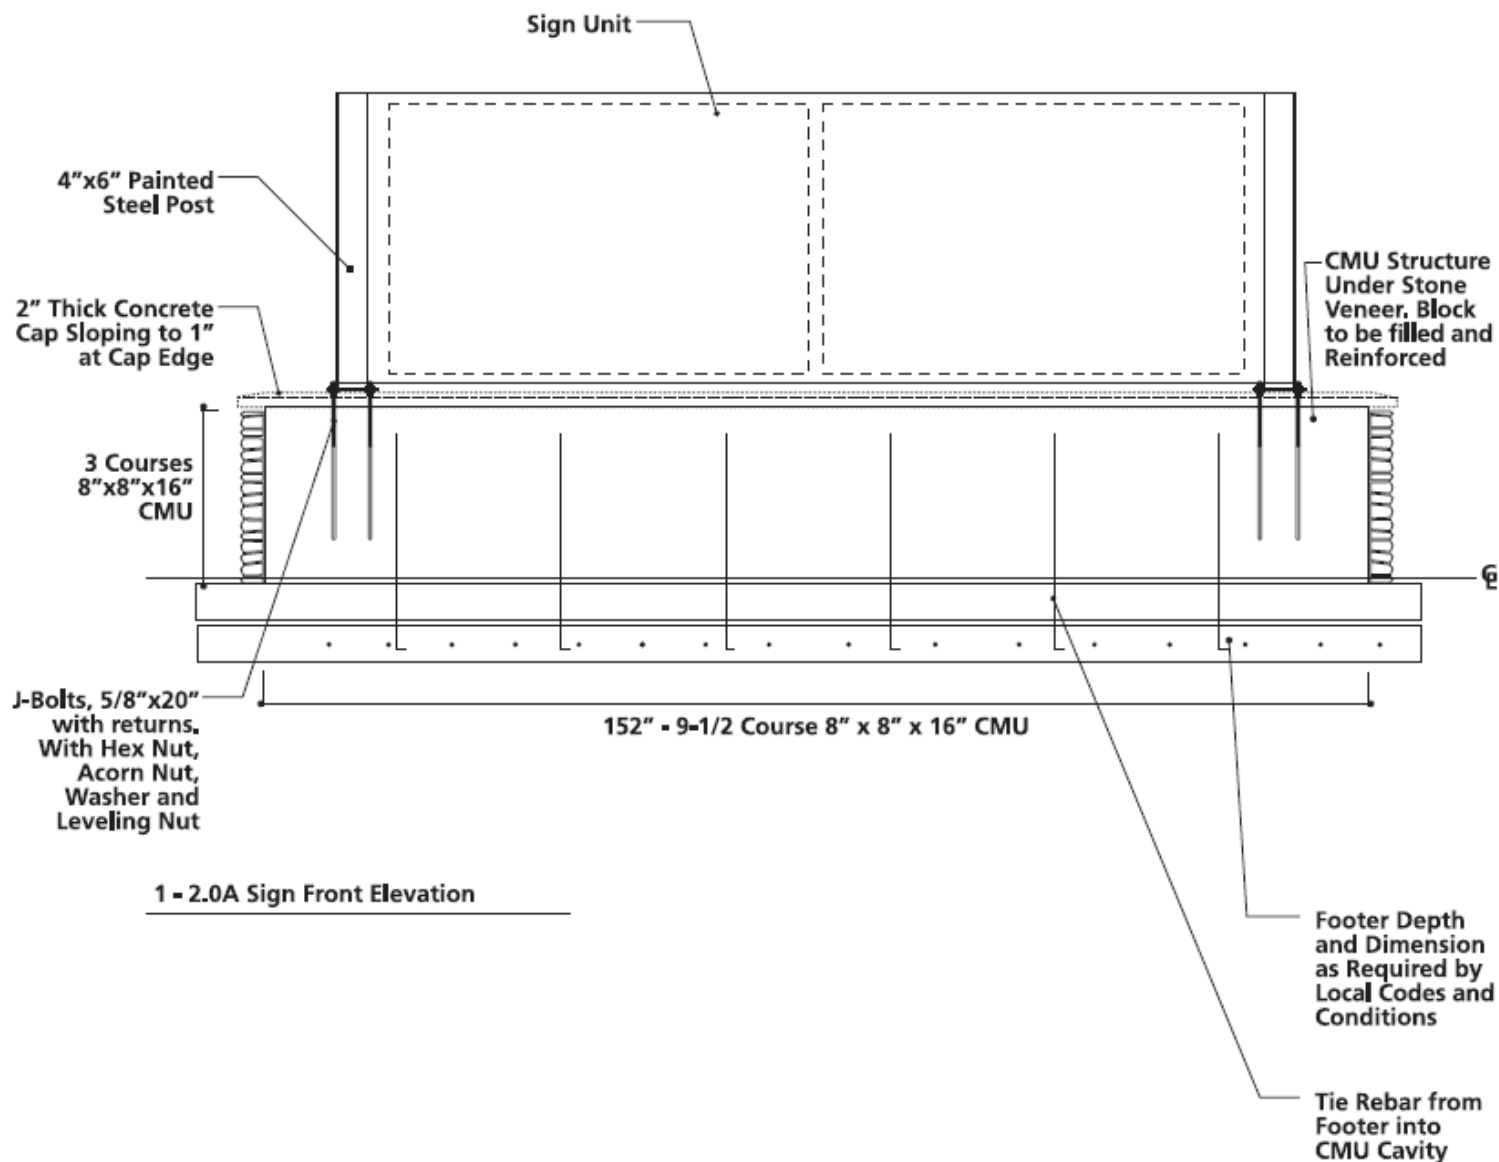

PROJECT

**FORT DONELSON
NATIONAL
HISTORIC SITE**

PROJECT NUMBER

0808-727-FODO

UNIT | AREA

Dover Hotel

DRAWING SCALE

1/2" = 1' - 0"

ENLARGE FOR FULL SCALE

2400%

SIGN CATEGORY

Identification

DESCRIPTION

STRUCTURE: QTY: 1
Stone Monolith Base, To Be Provided By Park

PANEL: QTY: 1
F/Pla1-1GA Per NPS Standards, 1-Sided Western Red Cedar with Blank Back, Routed Typography and Full-color Arrowhead, Per NPS Standards

DRAWING DATE

08-08-2008

REVISION | DATE

1

2

3


4

DRAWING NUMBER

2.0A | FODO



National Park Service
U.S. Department of the Interior
UniGuide Sign Program
304-635-4069

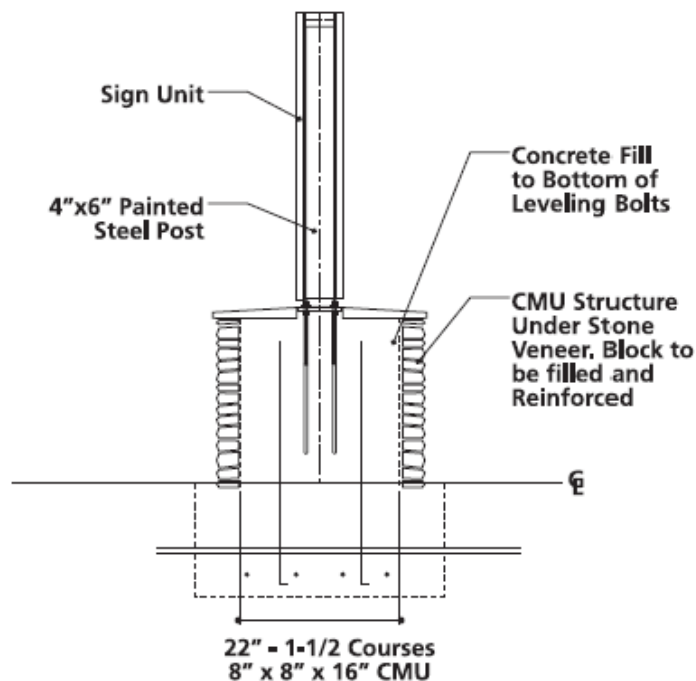

1 - 2.0B Sign Side Elevation

PROJECT

**FORT DONELSON
NATIONAL
HISTORIC SITE**

PROJECT NUMBER

0808-727-FODO

UNIT | AREA

Dover Hotel

DRAWING SCALE

1/2" = 1' - 0"

ENLARGE FOR FULL SCALE

2400%

SIGN CATEGORY

Identification

DESCRIPTION

STRUCTURE: QTY:
Stone Monolith Base, To Be
Provided By Park

PANEL: QTY: 1
F/Plaf-1GA Per NPS Standards,
1-Sided Western Red Cedar
with Blank Back, Routed
Typography and Full-color
Arrowhead, Per NPS Standards

DRAWING DATE

08-08-2008

REVISION | DATE

1

2

3


4

DRAWING NUMBER

2.0B | FODO



National Park Service
U.S. Department of the Interior
UniGuide Sign Program
304-635-4069

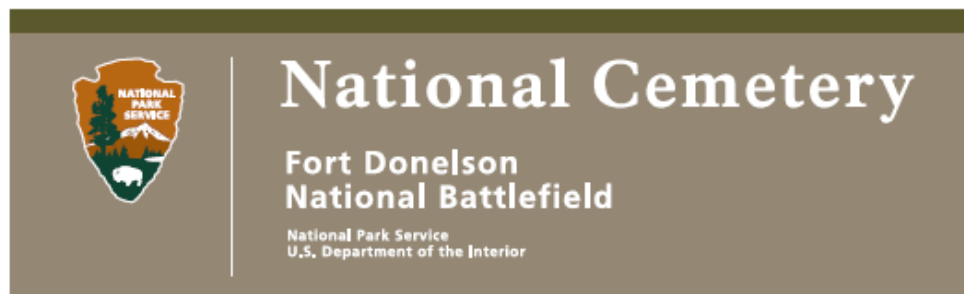

1 - 2.0C Front Sign Panel

Cap Height 6" - 132" x 39 3/4"

PROJECT

**FORT DONELSON
NATIONAL
HISTORIC SITE**

PROJECT NUMBER

0808-727-FODO

UNIT | AREA

Dover Hotel

DRAWING SCALE

1/2" = 1' - 0"

ENLARGE FOR FULL SCALE

2400%

SIGN CATEGORY

Identification

DESCRIPTION

STRUCTURE: QTY:
Stone Monolith Base, To Be
Provided By Park

PANEL: QTY: 1
F/Plaf-1GA Per NPS Standards,
1-Sided Western Red Cedar
with Blank Back, Routed
Typography and Full-color
Arrowhead, Per NPS Standards

DRAWING DATE

08-08-2008

REVISION | DATE

1	
2	
3	
4	

DRAWING NUMBER

2.0C | FODO



National Park Service
U.S. Department of the Interior
UniGuide Sign Program
304-635-4069



1 - 2.0D Back Sign Panel

132" x 39 3/4"

PROJECT

**FORT DONELSON
NATIONAL
HISTORIC SITE**

PROJECT NUMBER

0808-727-FODO

UNIT | AREA

Dover Hotel

DRAWING SCALE

1/2" = 1' - 0"

ENLARGE FOR FULL SCALE

2400%

SIGN CATEGORY

Identification

DESCRIPTION

STRUCTURE: **QTY:**
Stone Monolith Base, To Be
Provided By Park

PANEL: **QTY: 1**
F/Plaf-1GA Per NPS Standards,
1-Sided Western Red Cedar
with Blank Back, Routed
Typography and Full-color
Arrowhead, Per NPS Standards

DRAWING DATE

08-08-2008

REVISION | DATE

1	
2	
3	
4	

DRAWING NUMBER

2.0D | FODO



National Park Service
U.S. Department of the Interior
Unit/Guide Sign Program
304-635-4069


Fort Donelson National Battlefield

Park Identity Sign

February 6, 2008
0208-650-FODO



Office of NPS Identity
Harpers Ferry Center
Interpretive Design Center
Harpers Ferry, WV 25425
304-535-4069

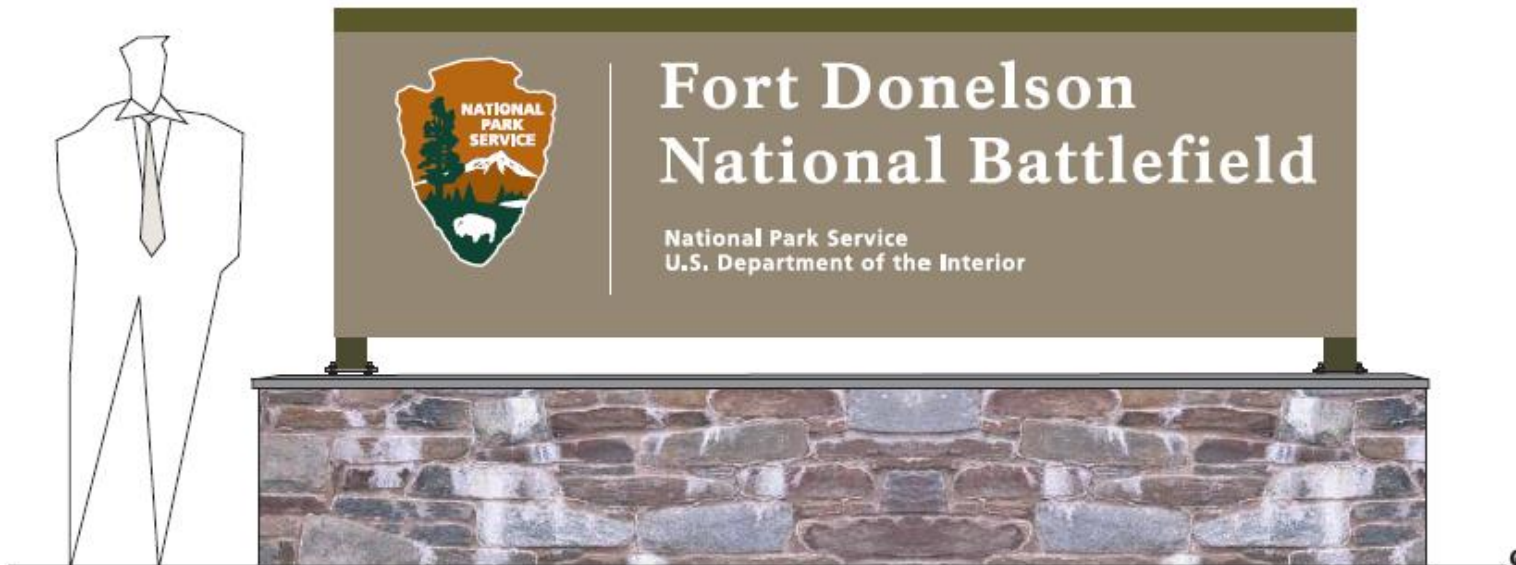

1 - 1.0 Park ID Stone Monolith 2-Sided - Cap Height 6" - 138" x 43-1/4"

PROJECT

**FORT DONELSON
NATIONAL BATTLEFIELD**

PROJECT NUMBER

0208-650-FODO

UNIT | AREA

Battlefield Entrance

DRAWING SCALE

1/2" = 1' - 0"

ENLARGE FOR FULL SCALE

2400%

SIGN CATEGORY

IDENTITY

DESCRIPTION

STRUCTURE: QTY: 1
Stone Monolith Base

PANEL: QTY: 2
Pla-2GA Per NPS Standards, 2-Sided Western Red Cedar with routed typography with full-color arrowhead.

DRAWING DATE

02-06-2008

REVISION | DATE

1

2

3


4

DRAWING NUMBER

1.0 | FODO



National Park Service
U.S. Department of the Interior
Interpretive Sign Program
304-635-6069

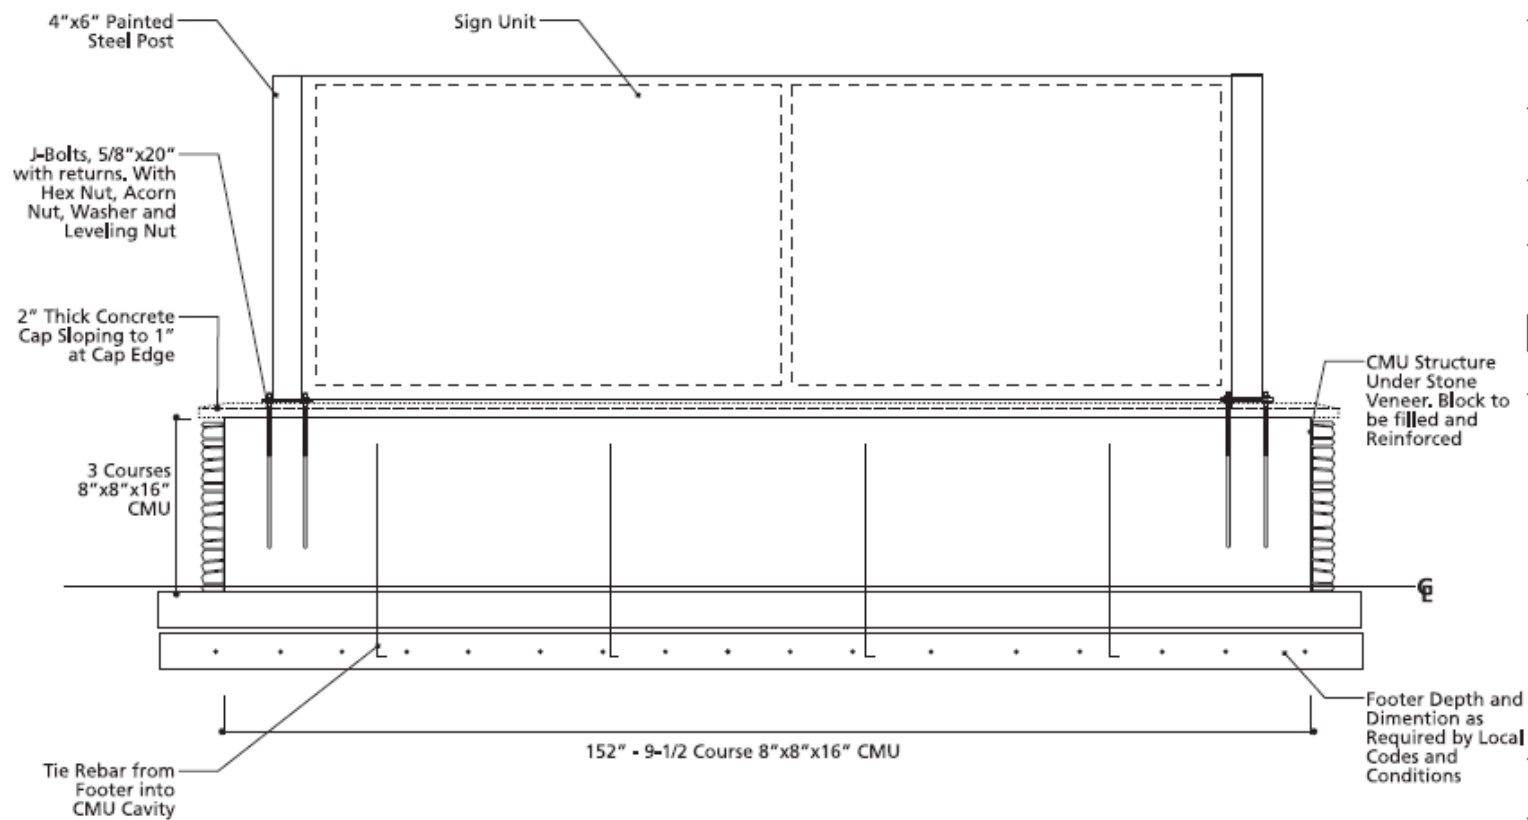

1 - 1.0A Sign Front Elevation

PROJECT

FORT DONELSON
NATIONAL BATTLEFIELD

PROJECT NUMBER

0208-650-FODO

UNIT | AREA

Battlefield Entrance

DRAWING SCALE

1/2" = 1' - 0"

ENLARGE FOR FULL SCALE

2400%

SIGN CATEGORY

IDENTITY

DESCRIPTION

STRUCTURE: QTY: 1
Stone Monolith Base

PANEL:

QTY: 2

DRAWING DATE

02-06-2008

REVISION | DATE

1

2

3


4

DRAWING NUMBER

1.0A | FODO



National Park Service
U.S. Department of the Interior
UniGuide Sign Program
304-635-6069

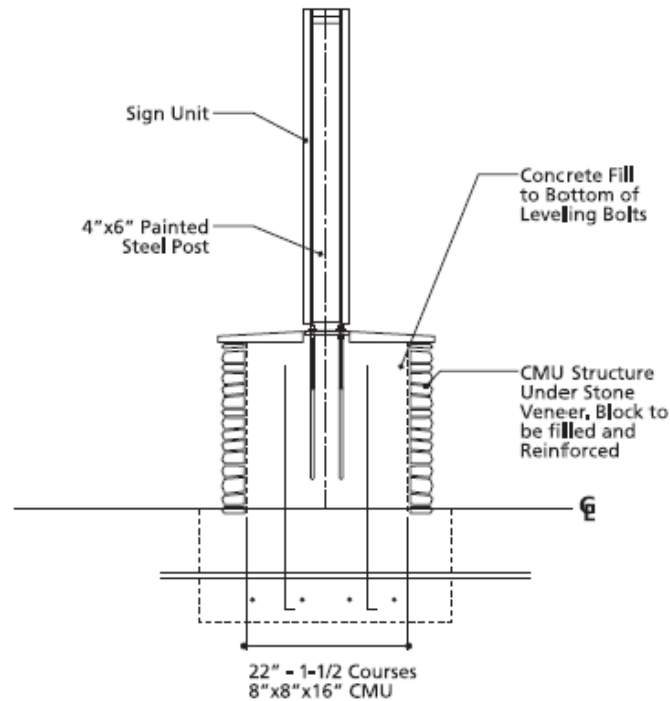

1 - 1.0B Sign Side Elevation

PROJECT

**FORT DONELSON
NATIONAL BATTLEFIELD**

PROJECT NUMBER

0208-650-FODO

UNIT | AREA

Battlefield Entrance

DRAWING SCALE

1/2" = 1' - 0"

ENLARGE FOR FULL SCALE

2400%

SIGN CATEGORY

IDENTITY

DESCRIPTION

STRUCTURE: QTY: 1
Stone Monolith Base

PANEL:

QTY:

DRAWING DATE

02-06-2008

REVISION | DATE


1	
2	
3	
4	

DRAWING NUMBER

1.0B | FODO



National Park Service
U.S. Department of the Interior
UniGuide Sign Program
304-635-4069

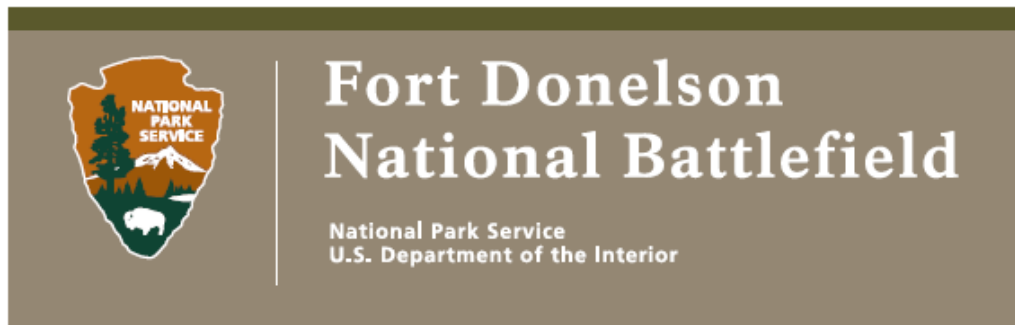

1 - 1.0C Sign Panel, Front and Back - Cap Height 6" - 138"x 43-1/4"

PROJECT

**FORT DONELSON
NATIONAL BATTLEFIELD**

PROJECT NUMBER

0208-650-FODO

UNIT | AREA

Battlefield Entrance

DRAWING SCALE

1/2" = 1' - 0"

ENLARGE FOR FULL SCALE

2400%

SIGN CATEGORY

IDENTITY

DESCRIPTION

STRUCTURE: QTY:

PANEL:

QTY: 2

Pla-2GA Per NPS Standards, 2-Sided Western Red Cedar with routed typography with full-color arrowhead.

DRAWING DATE

02-06-2008

REVISION | DATE

1	
2	
3	
4	

DRAWING NUMBER

1.0C | FODO



National Park Service
U.S. Department of the Interior
UniGuide Sign Program
304-635-4069