



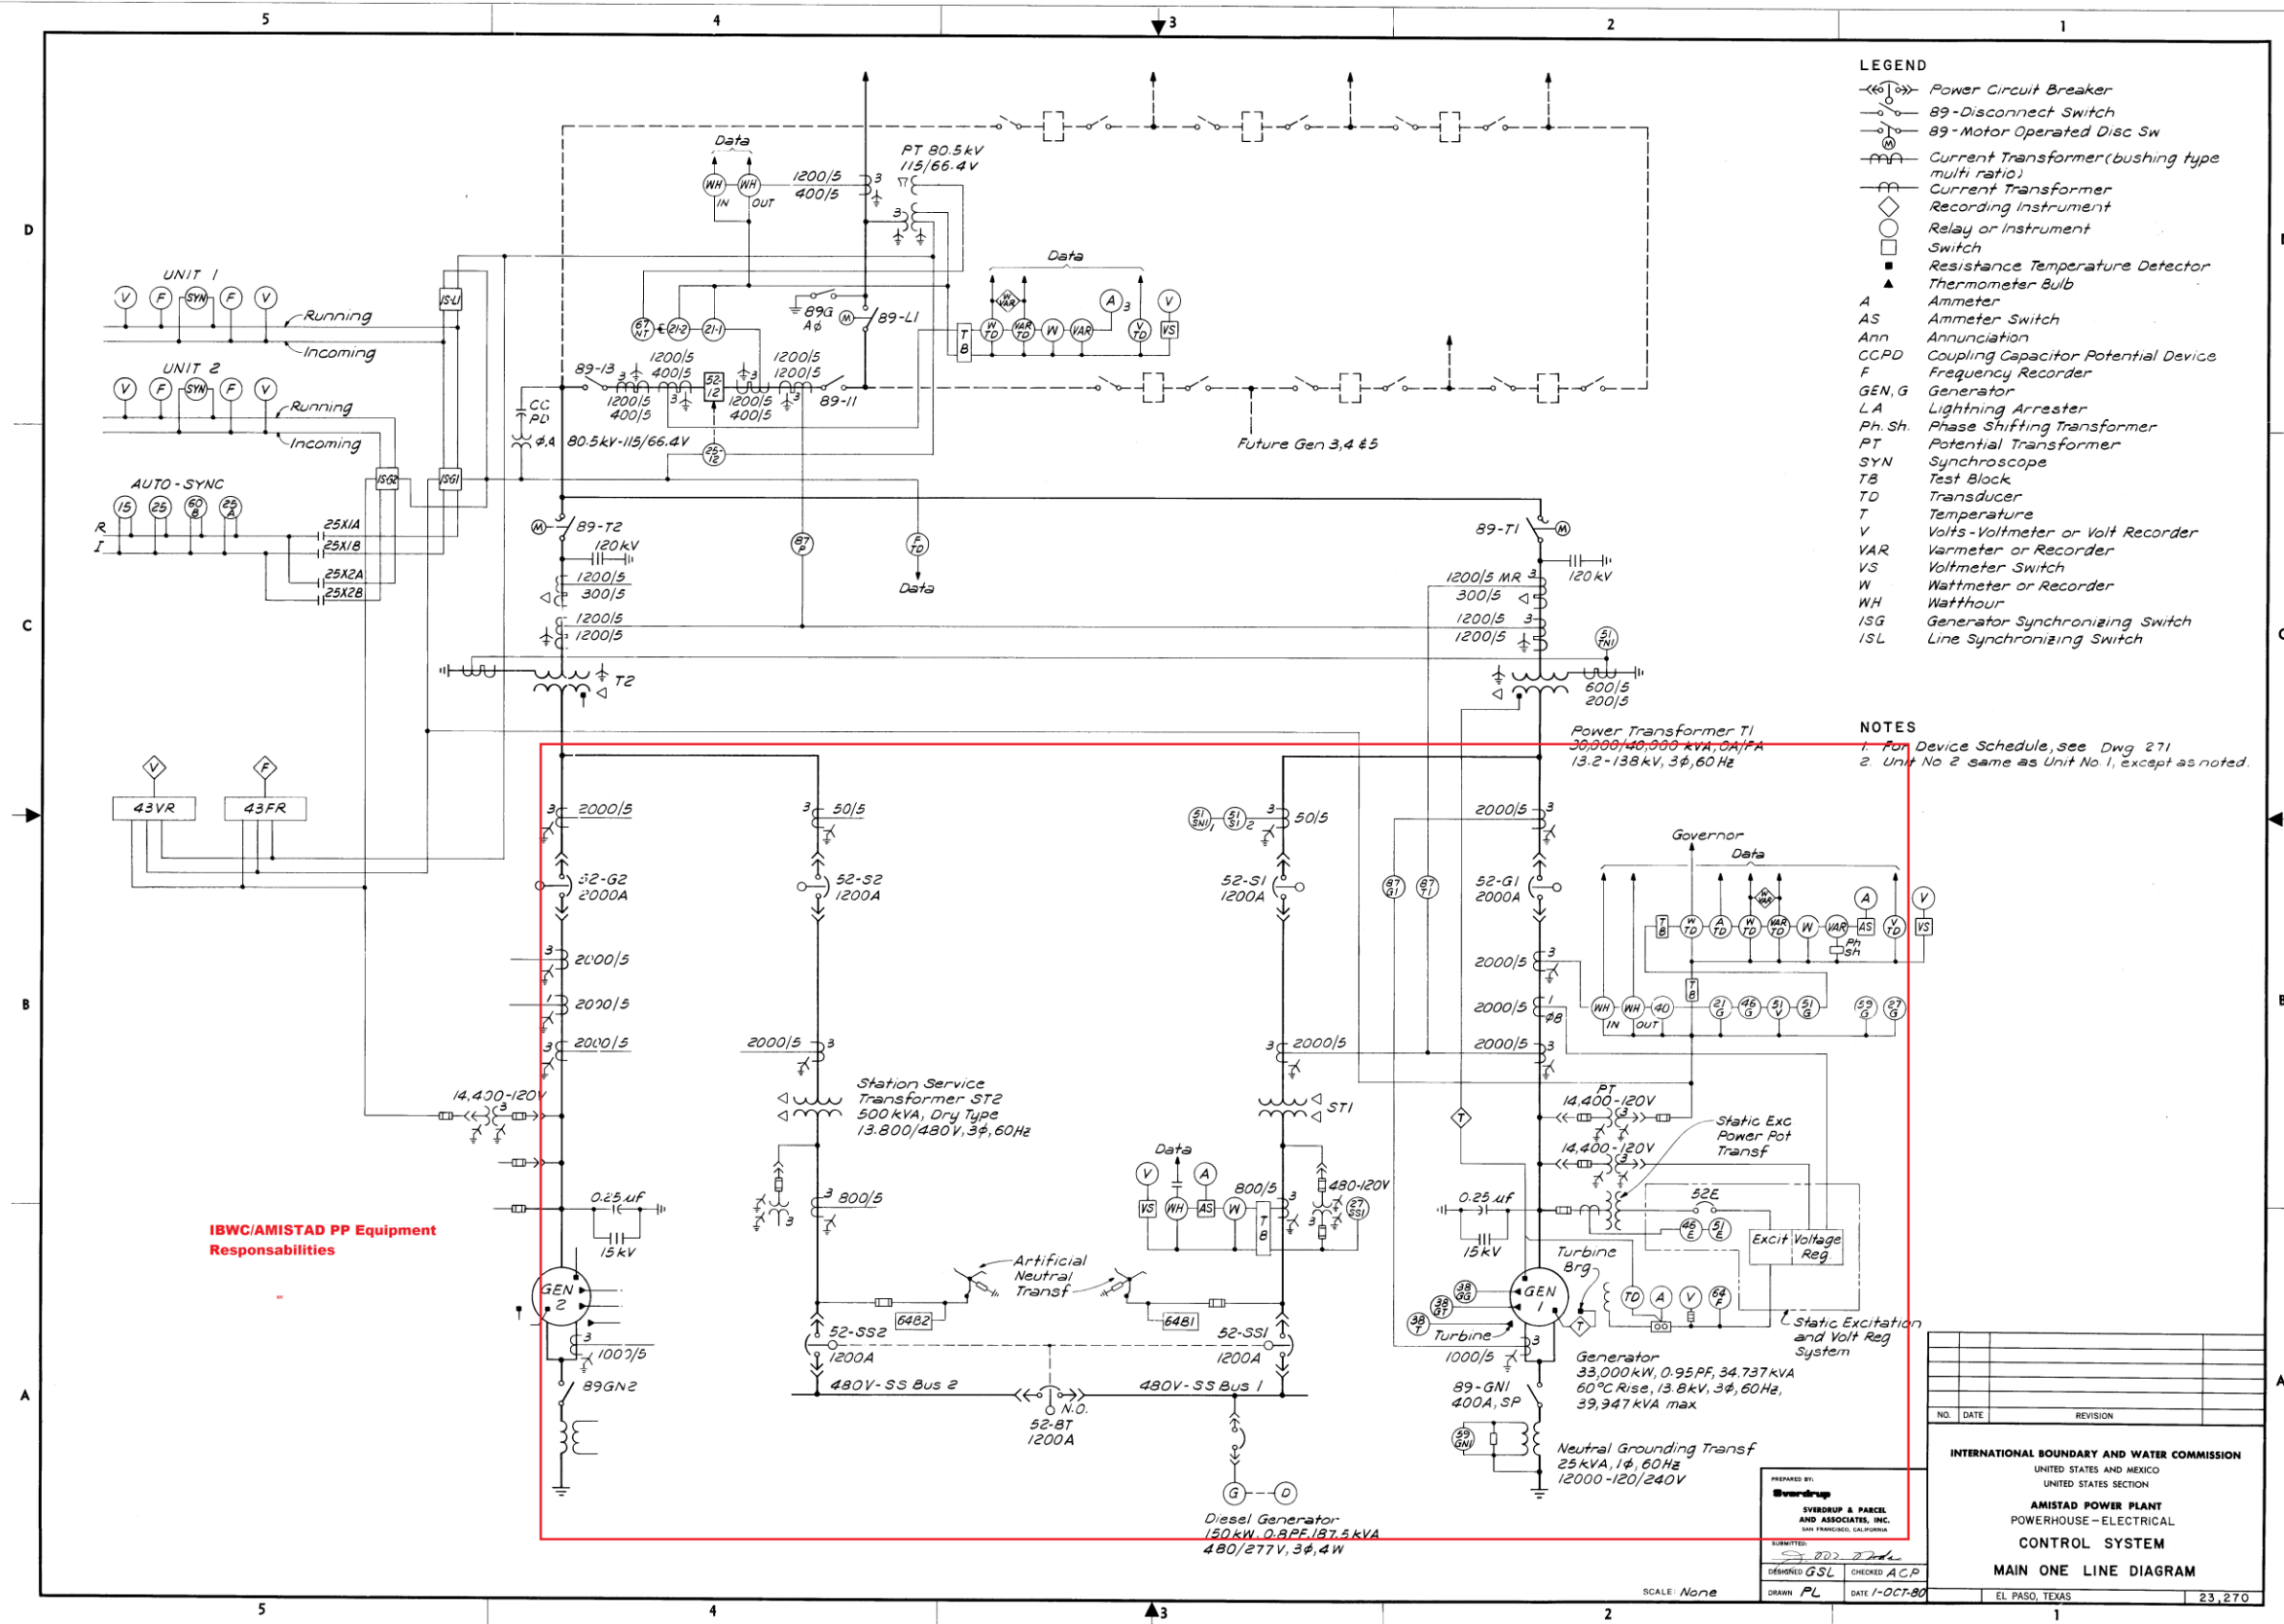

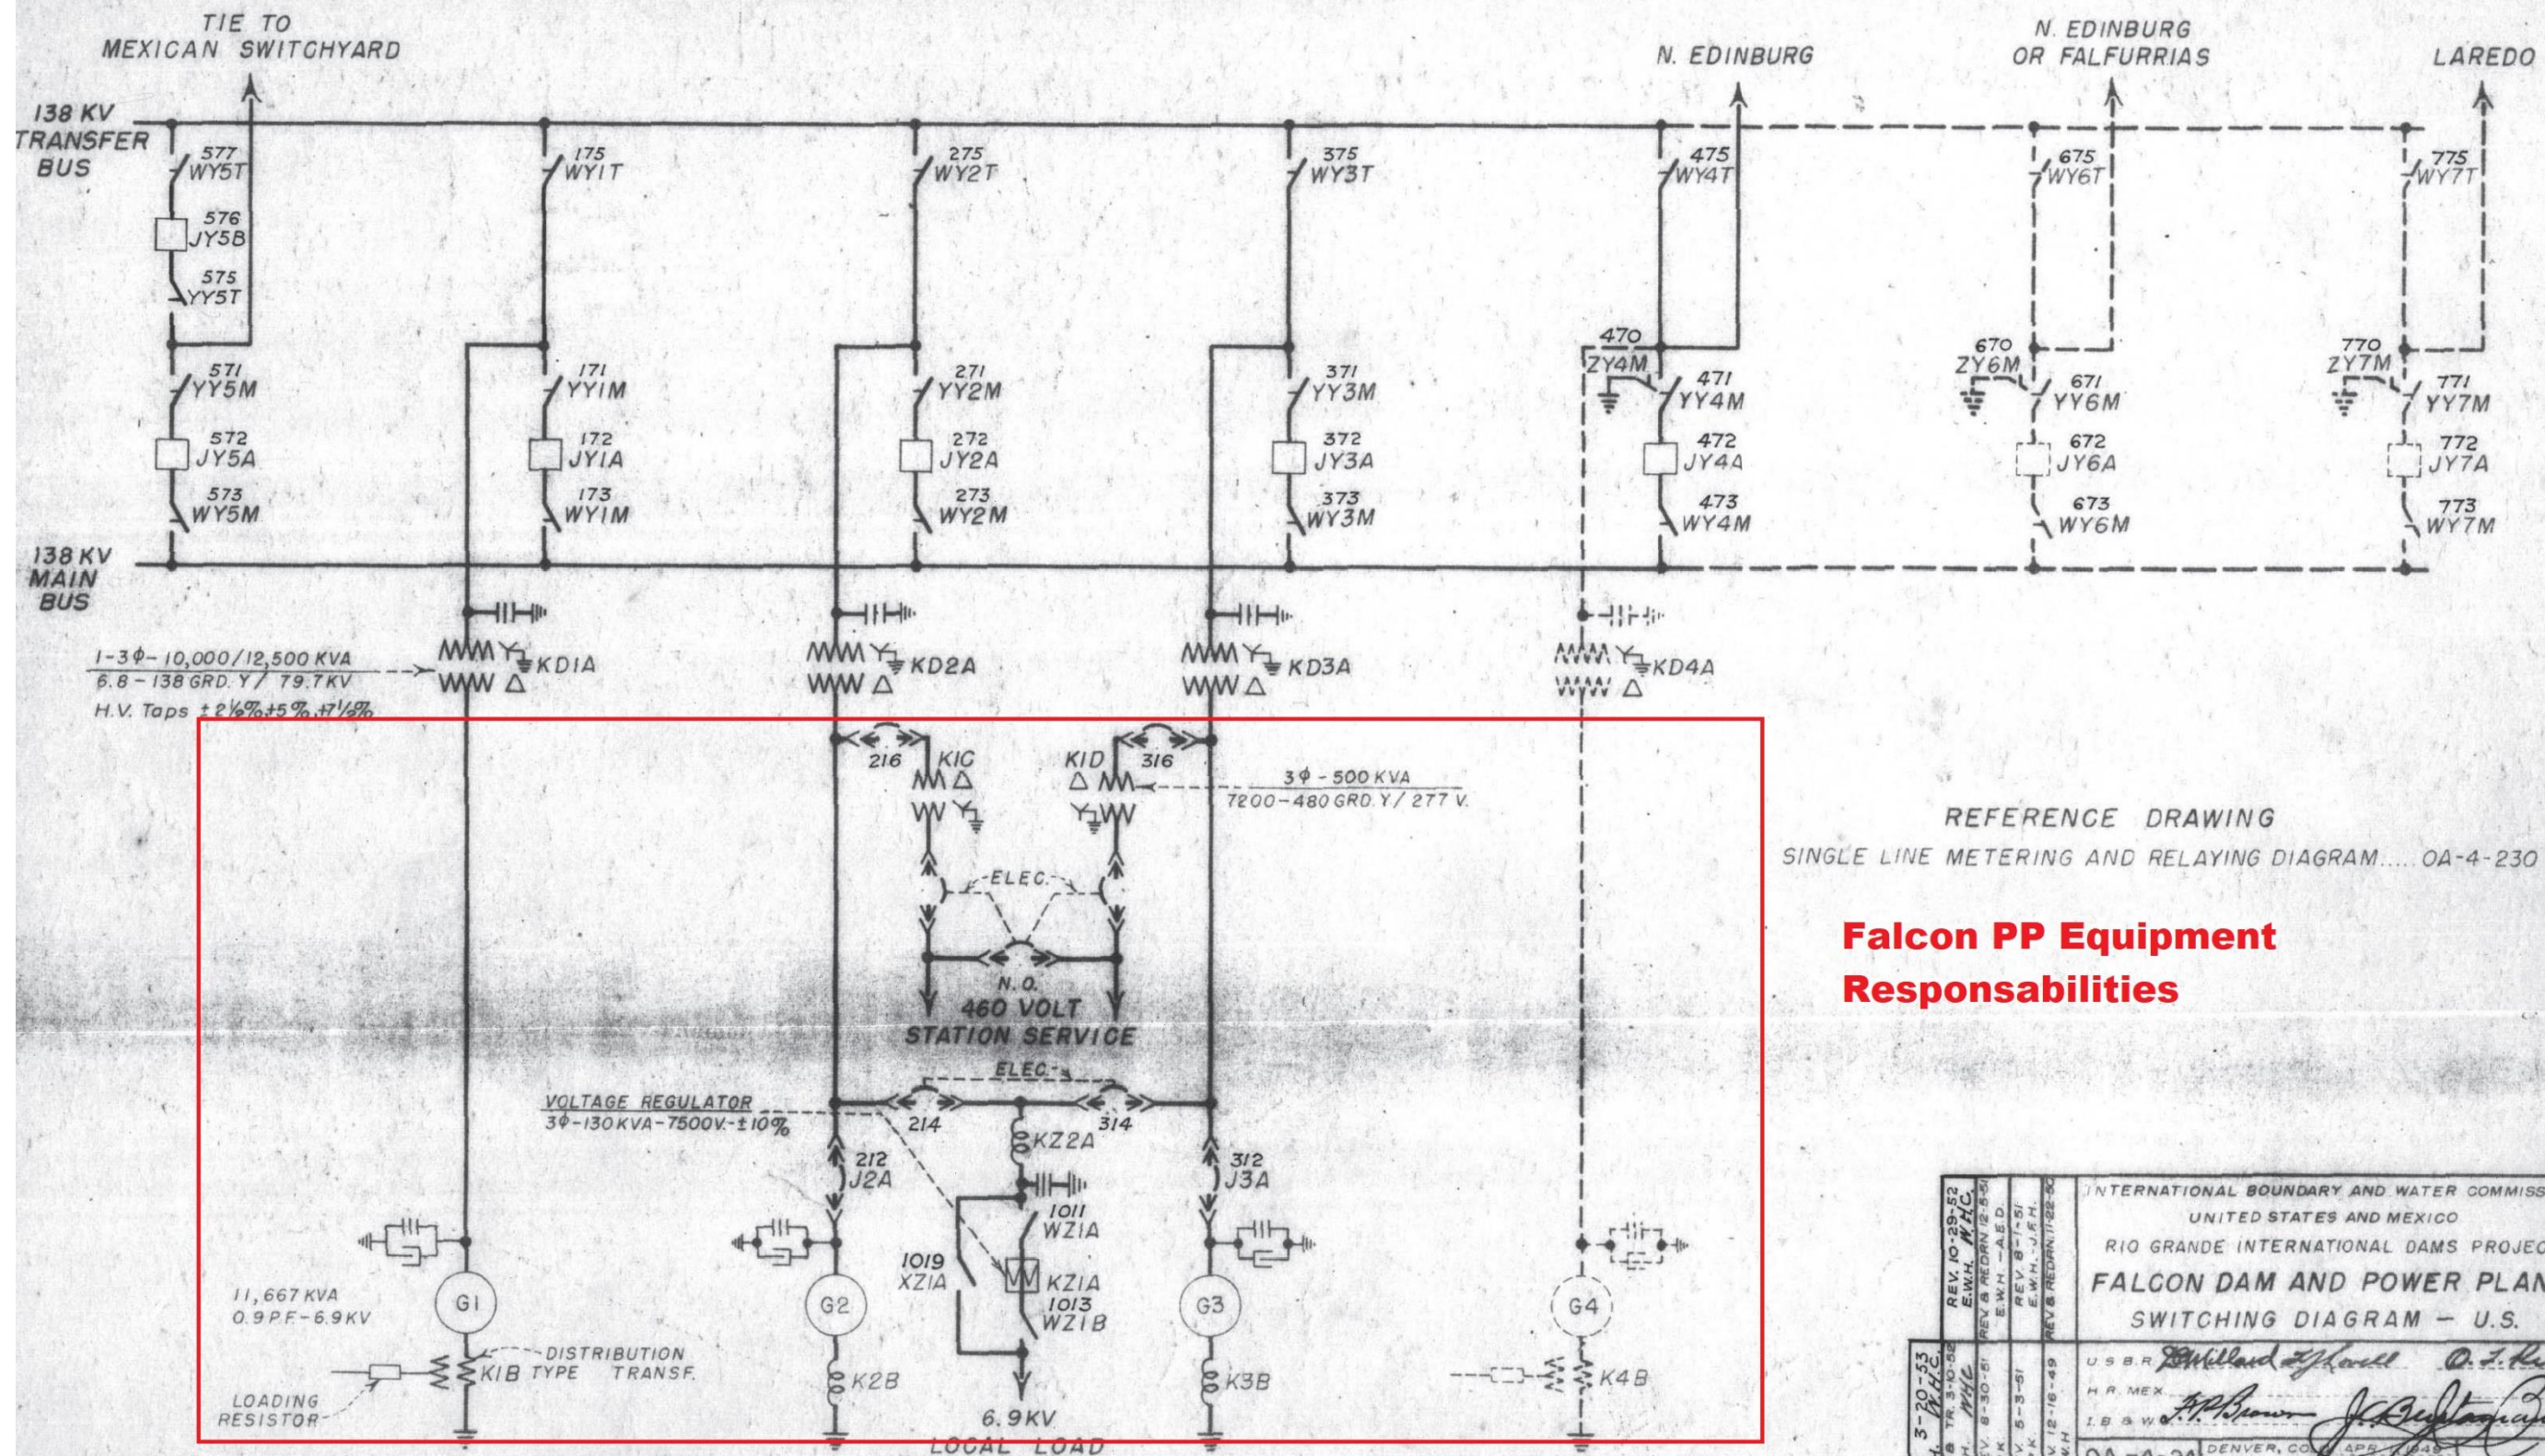

REFERENCE DRAWING
 SINGLE LINE METERING AND RELAYING DIAGRAM..... OA-4-230

Falcon PP Equipment Responsibilities

INTERNATIONAL BOUNDARY AND WATER COMMISSION UNITED STATES AND MEXICO RIO GRANDE INTERNATIONAL DAMS PROJECT FALCON DAM AND POWER PLANT SWITCHING DIAGRAM - U.S.			
REV. 5-20-53 E.W.H.	REV. 10-29-52 E.W.H.	REV. 8-30-51 J.P.K.	REV. 12-16-49 E.W.H.
U.S.B.R. <i>William J. Hall</i> H.R. MEX. <i>A.P. Brown</i> I.B. & W. <i>J. A. Quintanilla</i>	OA-4-24 DENVER, CO. APR. 1949 MEXICO, D. F. EL PASO & JUAREZ		
8979-135 DR. E.W.H. REJ. CK. R.B.G. W.S.			