

AMENDMENT OF SOLICITATION/MODIFICATION OF CONTRACT				1. CONTRACT ID CODE		PAGE OF PAGES	
				1		11	
2. AMENDMENT/MODIFICATION NO. AMDT 0003		3. EFFECTIVE DATE 11-Aug-2025		4. REQUISITION/PURCHASE REQ. NO. W22W9K51353222		5. PROJECT NO.(If applicable)	
6. ISSUED BY U. S. ARMY ENGINEER DISTRICT, LOUISVILLE 600 DR. MARTIN LUTHER KING, JR. PLACE ROOM 821 LOUISVILLE KY 40202-2239		CODE W912QR		7. ADMINISTERED BY (If other than item 6) See Item 6		CODE	
8. NAME AND ADDRESS OF CONTRACTOR (No., Street, County, State and Zip Code)				X		9A. AMENDMENT OF SOLICITATION NO. W912QR25B0053	
				X		9B. DATED (SEE ITEM 11) 27-Jun-2025	
						10A. MOD. OF CONTRACT/ORDER NO.	
						10B. DATED (SEE ITEM 13)	
CODE		FACILITY CODE					
11. THIS ITEM ONLY APPLIES TO AMENDMENTS OF SOLICITATIONS							
☒ The above numbered solicitation is amended as set forth in Item 14. The hour and date specified for receipt of Offer ☒ is extended, ☐ is not extended. Offer must acknowledge receipt of this amendment prior to the hour and date specified in the solicitation or as amended by one of the following methods: (a) By completing Items 8 and 15, and returning <u>1</u> copies of the amendment; (b) By acknowledging receipt of this amendment on each copy of the offer submitted; or (c) By separate letter or telegram which includes a reference to the solicitation and amendment numbers. FAILURE OF YOUR ACKNOWLEDGMENT TO BE RECEIVED AT THE PLACE DESIGNATED FOR THE RECEIPT OF OFFERS PRIOR TO THE HOUR AND DATE SPECIFIED MAY RESULT IN REJECTION OF YOUR OFFER. If by virtue of this amendment you desire to change an offer already submitted, such change may be made by telegram or letter, provided each telegram or letter makes reference to the solicitation and this amendment, and is received prior to the opening hour and date specified.							
12. ACCOUNTING AND APPROPRIATION DATA (If required)							
13. THIS ITEM APPLIES ONLY TO MODIFICATIONS OF CONTRACTS/ORDERS. IT MODIFIES THE CONTRACT/ORDER NO. AS DESCRIBED IN ITEM 14.							
A. THIS CHANGE ORDER IS ISSUED PURSUANT TO: (Specify authority) THE CHANGES SET FORTH IN ITEM 14 ARE MADE IN THE CONTRACT ORDER NO. IN ITEM 10A.							
B. THE ABOVE NUMBERED CONTRACT/ORDER IS MODIFIED TO REFLECT THE ADMINISTRATIVE CHANGES (such as changes in paying office, appropriation date, etc.) SET FORTH IN ITEM 14, PURSUANT TO THE AUTHORITY OF FAR 43.103(B).							
C. THIS SUPPLEMENTAL AGREEMENT IS ENTERED INTO PURSUANT TO AUTHORITY OF:							
D. OTHER (Specify type of modification and authority)							
E. IMPORTANT: Contractor ☐ is not, ☐ is required to sign this document and return _____ copies to the issuing office.							
14. DESCRIPTION OF AMENDMENT/MODIFICATION (Organized by UCF section headings, including solicitation/contract subject matter where feasible.) SEE SUMMARY OF CHANGES							
Except as provided herein, all terms and conditions of the document referenced in Item 9A or 10A, as heretofore changed, remains unchanged and in full force and effect.							
15A. NAME AND TITLE OF SIGNER (Type or print)				16A. NAME AND TITLE OF CONTRACTING OFFICER (Type or print)			
				TEL: _____ EMAIL: _____			
15B. CONTRACTOR/OFFEROR		15C. DATE SIGNED		16B. UNITED STATES OF AMERICA		16C. DATE SIGNED	
_____ (Signature of person authorized to sign)				BY _____ (Signature of Contracting Officer)			

SECTION SF 30 BLOCK 14 CONTINUATION PAGE

SUMMARY OF CHANGES

SECTION SF 30 - BLOCK 14 CONTINUATION PAGE (SF 30)

The following have been added by full text:

SUMMARY OF CHANGES ADMT 0003

P2#: 513984 HVAC & CONTROLS RENOVATION F/20824
WPAFB, OH
Amendment 003

The submission date is extended to 21 August 2025 at 10:00 AM EST. Acknowledgment of this amendment and proposals are due at that time

SUMMARY OF CHANGES

1. The following SPECIFICATION SECTIONS have been revised and replaced in their entirety:

None.

2. The following SPECIFICATION SECTIONS have been added in their entirety:

None.

3. The following SPECIFICATION SECTIONS have been deleted in their entirety:

None

4. The following PLAN SHEETS have been revised and replaced in their entirety:

ED210 LEVEL 1 OVERALL - DEMO LIGHTING PLAN
ED211 LEVEL 1 WEST- DEMO LIGHTING PLAN
ED212 LEVEL 1 EAST - DEMO LIGHTING PLAN
ED220 LEVEL 2 – DEMO LIGHTING PLAN
E-210 LEVEL 1 WEST LIGHTING PLAN
E-601 ELECTRICAL SCHEDULES
E-602 ELECTRICAL SCHEDULES
E-604 ELECTRICAL PANEL SCHEDULES

5. The following PLAN SHEETS have been added new:

None.

6. The following PLAN SHEETS have been deleted in their entirety new:

None.

7. The following DOCUMENTS have been replaced in their entirety:

None.

8. The Construction Wage Rates have been replaced in their entirety.

SECTION 00 10 00 - SOLICITATION

The required response date/time has changed from 12-Aug-2025 01:00 PM to 21-Aug-2025 10:00 AM.

SECTION 00 73 00 - SUPPLEMENTARY CONDITIONS

The following have been modified:

WAGE RATES

"General Decision Number: OH20250081 07/25/2025

Superseded General Decision Number: OH20240081

State: Ohio

Construction Type: Building

County: Greene County in Ohio.

BUILDING CONSTRUCTION PROJECTS (does not include single family homes or apartments up to and including 4 stories).

Note: Contracts subject to the Davis-Bacon Act are generally required to pay at least the applicable minimum wage rate required under Executive Order 14026 or Executive Order 13658. Please note that these Executive Orders apply to covered contracts entered into by the federal government that are subject to the Davis-Bacon Act itself, but do not apply to contracts subject only to the Davis-Bacon Related Acts, including those set forth at 29 CFR 5.1(a)(1).

If the contract is entered into on or after January 30, 2022, or the contract is renewed or extended (e.g., an option is exercised) on or after January 30, 2022:	. Executive Order 14026 generally applies to the contract. The contractor must pay all covered workers at least \$17.75 per hour (or the applicable wage rate listed on this wage determination, if it is higher) for all hours spent performing on the contract in 2025.
If the contract was awarded on or between January 1, 2015 and January 29, 2022, and the contract is not renewed or	. Executive Order 13658 generally applies to the contract. The contractor must pay all

extended on or after January 30, 2022:	covered workers at least \$13.30 per hour (or the applicable wage rate listed on this wage determination, if it is higher) for all hours spent performing on that contract in 2025.
--	---

The applicable Executive Order minimum wage rate will be adjusted annually. If this contract is covered by one of the Executive Orders and a classification considered necessary for performance of work on the contract does not appear on this wage determination, the contractor must still submit a conformance request.

Additional information on contractor requirements and worker protections under the Executive Orders is available at <http://www.dol.gov/whd/govcontracts>.

Modification Number	Publication Date
0	01/03/2025
1	02/07/2025
2	02/14/2025
3	03/14/2025
4	04/25/2025
5	05/30/2025
6	06/06/2025
7	07/18/2025
8	07/25/2025

ASBE0008-010 03/01/2025

	Rates	Fringes
ASBESTOS WORKER/HEAT & FROST INSULATOR.....	\$ 35.23	23.04

BROH0018-003 06/01/2024		

	Rates	Fringes
BRICKLAYER.....	\$ 33.30	18.28

BROH0022-010 07/01/2024		

	Rates	Fringes
TILE FINISHER.....	\$ 28.28	11.05
TILE SETTER.....	\$ 30.98	15.82

* CARP0002-017 06/01/2025		

	Rates	Fringes
CARPENTER.....	\$ 30.96	18.44

ELEC0082-004 12/02/2024

	Rates	Fringes
ELECTRICIAN.....	\$ 38.00	22.49

ELEV0011-002 01/01/2025

	Rates	Fringes
ELEVATOR MECHANIC.....	\$ 57.41	38.435+a+b

PAID HOLIDAYS:

a. New Year's Day, Memorial Day, Independence Day, Labor Day, Vetern's Day, Thanksgiving Day, the Friday after Thanksgiving, and Christmas Day.

b. Employer contributes 8% of regular hourly rate to vacation pay credit for employee who has worked in business more than 5 years; 6% for less than 5 years' service.

ENGI0018-034 05/01/2024

	Rates	Fringes
POWER EQUIPMENT OPERATOR Crane.....	\$ 44.14	16.41

ENGI0066-045 06/01/2017

	Rates	Fringes
POWER EQUIPMENT OPERATOR Forklift.....	\$ 28.87	19.66
Grader/Blade.....	\$ 32.42	19.66
Mechanic.....	\$ 32.92	19.66

IRON0044-020 06/01/2025

	Rates	Fringes
IRONWORKER, ORNAMENTAL.....	\$ 38.27	23.90

IRON0290-006 06/01/2024

	Rates	Fringes
IRONWORKER (Reinforcing and		

Structural).....\$ 35.39 24.35

LABO0265-018 06/01/2024

Rates Fringes

LABORER

Mason Tender - Brick.....\$ 25.90 18.40

LABO1410-004 04/01/2024

Rates Fringes

LABORER

Common or General;
Asbestos Abatement
(Removal from Ceilings,
Floors, and Walls).....\$ 31.65 12.95

PAIN0249-005 05/01/2025

Rates Fringes

PAINTER (Brush and Roller).....\$ 29.15 13.97

PAIN0387-002 11/01/2023

Rates Fringes

GLAZIER.....\$ 31.95 18.20

* PLAS0132-020 06/01/2025

Rates Fringes

CEMENT MASON/CONCRETE FINISHER...\$ 32.71 19.27

PLUM0050-009 06/30/2025

Rates Fringes

PIPEFITTER (Excludes HVAC
Pipe Installation).....\$ 51.00 32.56

PLUM0162-009 06/01/2024

Rates Fringes

PLUMBER (Includes HVAC Pipe
Installation).....\$ 43.05 27.18

ROOF0042-001 08/01/2024

Rates Fringes

ROOFER.....\$ 33.00 19.42

SFOH0669-009 01/01/2025

Rates Fringes

SPRINKLER FITTER (Fire
Sprinklers).....\$ 45.11 28.08

* UAVG-OH-0021 01/01/2019

Rates Fringes

OPERATOR: Oiler.....\$ 27.56 16.37

* UAVG-OH-0025 01/01/2018

Rates Fringes

SHEET METAL WORKER, Excludes
HVAC Duct and Unit
Installation.....\$ 28.10 23.41

* UAVG-OH-0027 01/01/2018

Rates Fringes

OPERATOR:
Backhoe/Excavator/Trackhoe.....\$ 34.84 14.76

SUOH2012-083 08/29/2014

Rates Fringes

DRYWALL HANGER AND METAL STUD
INSTALLER.....\$ 21.02 4.21

FORM WORKER.....\$ 22.41 9.01

LABORER: Mason Tender -
Cement/Concrete.....\$ 22.95 8.60

LABORER: Pipelayer.....\$ 23.98 8.58

OPERATOR: Bobcat/Skid
Steer/Skid Loader.....\$ 30.26 12.58

OPERATOR: Bulldozer.....\$ 26.01 4.95

OPERATOR: Loader.....\$ 29.99 12.80

OPERATOR: Paver (Asphalt,
Aggregate, and Concrete).....\$ 30.28 13.29

OPERATOR: Roller.....\$ 28.25 12.61

PAINTER: Spray.....\$ 22.78 12.40

SHEET METAL WORKER (HVAC Duct
and HVAC Unit Installation
Only).....\$ 26.41 17.34

TRUCK DRIVER: Dump (All Types)...\$ 22.08 11.51

WELDERS - Receive rate prescribed for craft performing
operation to which welding is incidental.

=====

Note: Executive Order (EO) 13706, Establishing Paid Sick Leave for Federal Contractors applies to all contracts subject to the Davis-Bacon Act for which the contract is awarded (and any solicitation was issued) on or after January 1, 2017. If this contract is covered by the EO, the contractor must provide employees with 1 hour of paid sick leave for every 30 hours they work, up to 56 hours of paid sick leave each year. Employees must be permitted to use paid sick leave for their own illness, injury or other health-related needs, including preventive care; to assist a family member (or person who is like family to the employee) who is ill, injured, or has other health-related needs, including preventive care; or for reasons resulting from, or to assist a family member (or person who is like family to the employee) who is a victim of, domestic violence, sexual assault, or stalking. Additional information on contractor requirements and worker protections under the EO is available at <https://www.dol.gov/agencies/whd/government-contracts>.

Unlisted classifications needed for work not included within the scope of the classifications listed may be added after award only as provided in the labor standards contract clauses (29CFR 5.5 (a) (1) (iii)).

The body of each wage determination lists the classifications and wage rates that have been found to be prevailing for the type(s) of construction and geographic area covered by the wage determination. The classifications are listed in alphabetical order under rate identifiers indicating whether the particular rate is a union rate (current union negotiated rate), a survey rate, a weighted union average rate, a state adopted rate, or a supplemental classification rate.

Union Rate Identifiers

A four-letter identifier beginning with characters other than ""SU"", ""UAVG"", ?SA?, or ?SC? denotes that a union rate was prevailing for that classification in the survey. Example: PLUM0198-005 07/01/2024. PLUM is an identifier of the union whose collectively bargained rate prevailed in the survey for this classification, which in this example would be Plumbers. 0198 indicates the local union number or district council number where applicable, i.e., Plumbers Local 0198. The next number, 005 in the example, is an internal number used in processing the wage determination. The date, 07/01/2024 in the example, is the effective date of the most current negotiated rate.

Union prevailing wage rates are updated to reflect all changes over time that are reported to WHD in the rates in the collective bargaining agreement (CBA) governing the classification.

Union Average Rate Identifiers

The UAVG identifier indicates that no single rate prevailed for those classifications, but that 100% of the data reported for the classifications reflected union rates. EXAMPLE: UAVG-OH-0010 01/01/2024. UAVG indicates that the rate is a weighted union average rate. OH indicates the State of Ohio. The next number, 0010 in the example, is an internal number used in producing the wage determination. The date, 01/01/2024 in the example, indicates the date the wage determination was updated to reflect the most current union average rate.

A UAVG rate will be updated once a year, usually in January, to reflect a weighted average of the current rates in the collective bargaining agreements on which the rate is based.

Survey Rate Identifiers

The ""SU"" identifier indicates that either a single non-union rate prevailed (as defined in 29 CFR 1.2) for this classification in the survey or that the rate was derived by computing a weighted average rate based on all the rates reported in the survey for that classification. As a weighted average rate includes all rates reported in the survey, it may include both union and non-union rates. Example: SUFL2022-007 6/27/2024. SU indicates the rate is a single non-union prevailing rate or a weighted average of survey data for that classification. FL indicates the State of Florida. 2022 is the year of the survey on which these classifications and rates are based. The next number, 007 in the example, is an internal number used in producing the wage determination. The date, 6/27/2024 in the example, indicates the survey completion date for the classifications and rates under that identifier.

?SU? wage rates typically remain in effect until a new survey

is conducted. However, the Wage and Hour Division (WHD) has the discretion to update such rates under 29 CFR 1.6(c)(1).

State Adopted Rate Identifiers

The "SA" identifier indicates that the classifications and prevailing wage rates set by a state (or local) government were adopted under 29 C.F.R 1.3(g)-(h). Example: SAME2023-007 01/03/2024. SA reflects that the rates are state adopted. ME refers to the State of Maine. 2023 is the year during which the state completed the survey on which the listed classifications and rates are based. The next number, 007 in the example, is an internal number used in producing the wage determination. The date, 01/03/2024 in the example, reflects the date on which the classifications and rates under the "SA" identifier took effect under state law in the state from which the rates were adopted.

WAGE DETERMINATION APPEALS PROCESS

1) Has there been an initial decision in the matter? This can be:

- a) a survey underlying a wage determination
- b) an existing published wage determination
- c) an initial WHD letter setting forth a position on a wage determination matter
- d) an initial conformance (additional classification and rate) determination

On survey related matters, initial contact, including requests for summaries of surveys, should be directed to the WHD Branch of Wage Surveys. Requests can be submitted via email to davisbaconinfo@dol.gov or by mail to:

Branch of Wage Surveys
Wage and Hour Division
U.S. Department of Labor
200 Constitution Avenue, N.W.
Washington, DC 20210

Regarding any other wage determination matter such as conformance decisions, requests for initial decisions should be directed to the WHD Branch of Construction Wage Determinations. Requests can be submitted via email to BCWD-Office@dol.gov or by mail to:

Branch of Construction Wage Determinations
Wage and Hour Division
U.S. Department of Labor
200 Constitution Avenue, N.W.
Washington, DC 20210

2) If an initial decision has been issued, then any interested party (those affected by the action) that disagrees with the decision can request review and reconsideration from the Wage and Hour Administrator (See 29 CFR Part 1.8 and 29 CFR Part 7). Requests for review and reconsideration can be submitted via email to dba.reconsideration@dol.gov or by mail to:

Wage and Hour Administrator
U.S. Department of Labor
200 Constitution Avenue, N.W.
Washington, DC 20210

The request should be accompanied by a full statement of the interested party's position and any information (wage payment data, project description, area practice material, etc.) that the requestor considers relevant to the issue.

3) If the decision of the Administrator is not favorable, an interested party may appeal directly to the Administrative Review Board (formerly the Wage Appeals Board). Write to:

Administrative Review Board
U.S. Department of Labor
200 Constitution Avenue, N.W.
Washington, DC 20210.

=====

END OF GENERAL DECISION"

(End of Summary of Changes)

G

F

E

D

C

B

A

GENERAL NOTES

1. REFER TO SHEET E-001 FOR GENERAL NOTES, ABBREVIATIONS, AND SYMBOLS.
2. EXISTING CONDUIT PATHWAYS AND DEVICE AND LIGHTING BACKBOX SHALL REMAIN FOR REUSE WHERE POSSIBLE. ALL WIRING AND CABLING SHALL BE REMOVED BACK TO THE SOURCE UNLESS NOTED OTHERWISE.
3. A DASHED FIXTURE INDICATES THAT THE FIXTURE IS TO BE DEMOLISHED AND A FIXTURE THAT IS SOLID IS EXISTING TO REMAIN.

HAZARDOUS MATERIALS DEMOLITION - GENERAL NOTES

- A. ANALYTICAL RESULTS INDICATE THAT ASBESTOS IS PRESENT IN THE TSI PIPE WRAP.
- B. SURVEY RESULTS OBSERVED 13 POTENTIAL MERCURY CONTAINING DEVICES, INCLUDING THERMOSTATS THROUGHOUT THE BUILDINGS AND THERMOMETERS ASSOCIATED WITH THE BUILDING'S AIR HANDLERS.
- C. ALL FLUORESCENT LIGHTS SHOULD BE ASSUMED TO BE MERCURY CONTAINING AND ALL LIGHT BALLASTS ASSUMED TO CONTAIN PCBs
- D. LEAD BASED PAINT (LBP), OF THE 41 DATA POINTS COLLECTED THROUGHOUT THE BUILDING, NONE WERE FOUND TO CONTAIN LBP 1mg/cm2.

* ALL HAZARDOUS MATERIALS SHOULD BE HANDLED IN ACCORDANCE WITH REQUIREMENTS.


KEY NOTES

1. ALL LIGHTS IN THIS AREA ARE TO BE REMOVED, STORED, AND REINSTALLED UPON COMPLETION OF HVAC RENOVATION.
2. ALL LIGHTS IN THIS AREA ARE TO BE DEMOLISHED



1 LEVEL 1 - LIGHTING DEMO PLAN

ED210 / SCALE: 1/16" = 1'-0"

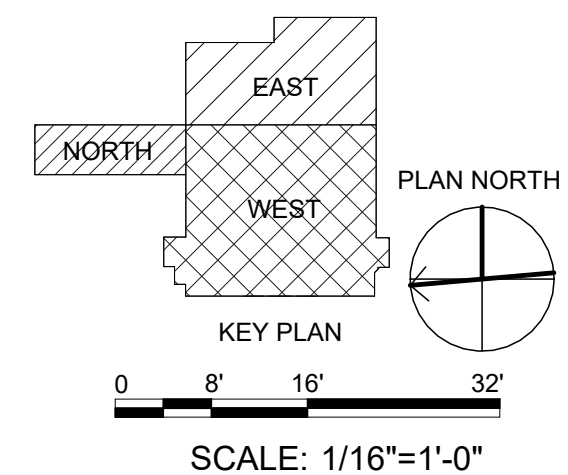

ISSUE DATE:

19 MARCH 2025
SOLICITATION NO.:

CONTRACT NO.:

DESIGNED BY:

J. HOOVER
DRAWN BY:

A. TYLER
CHECKED BY:
C. BARNES

R. BARNARD
SUBMITTED BY:
S. DICKINSON

D. RICHTER	SIZE: ANSI D
------------	-----------------

US ARMY CORPS OF ENGINEERS
LOUISVILLE DISTRICT
300 DB MARTIN LUTHER KING JR BLVD
LOUISVILLE, KY 40203

TETRA TECH

WRIGHT-PATTERSON AIR FORCE BASE, OHIO
HVAC & CONTROLS RENOVATION F/20824
FY2026

LEVEL 1 OVERALL - DEMO LIGHTING PLAN

SHEET ID

ED210

W912QR25B0053 Plans-0003

CERTIFIED FINAL



G

F

E

D

C

B

A

GENERAL NOTES

1. REFER TO SHEET E-001 FOR GENERAL NOTES, ABBREVIATIONS, AND SYMBOLS.
2. EXISTING CONDUIT PATHWAYS AND DEVICE AND LIGHTING BACKBOXES SHALL REMAIN FOR REUSE WHERE POSSIBLE. ALL WIRING AND CABLING SHALL BE REMOVED BACK TO THE SOURCE UNLESS NOTED OTHERWISE.
3. A DASHED FUTURE INDICATES THAT THE FUTURE IS TO BE DEMOLISHED AND A FUTURE THAT IS SOLID IS EXISTING TO REMAIN.


HAZARDOUS MATERIALS DEMOLITION - GENERAL NOTES

- A. ANALYTICAL RESULTS INDICATE THAT ASBESTOS IS PRESENT IN THE TSI PIPE WRAP.
- B. SURVEY RESULTS OBSERVED 13 POTENTIAL MERCURY CONTAINING DEVICES, INCLUDING THERMOSTATS THROUGHOUT THE BUILDINGS AND THERMOMETERS ASSOCIATED WITH THE BUILDING'S AIR HANDLERS.
- C. ALL FLUORESCENT LIGHTS SHOULD BE ASSUMED TO BE MERCURY CONTAINING AND ALL LIGHT BALLASTS ASSUMED TO CONTAIN PCBs
- D. LEAD BASED PAINT (LBP), OF THE 41 DATA POINTS COLLECTED THROUGHOUT THE BUILDING, NONE WERE FOUND TO CONTAIN LBP 1mg/cm2.



* ALL HAZARDOUS MATERIALS SHOULD BE HANDLED IN ACCORDANCE WITH REQUIREMENTS.

KEY NOTES

1. ALL LIGHTS IN THIS AREA ARE TO BE REMOVED, STORED, AND REINSTALLED UPON COMPLETION OF HVAC RENOVATION.
2. ALL LIGHTS IN THIS AREA ARE TO BE DEMOLISHED

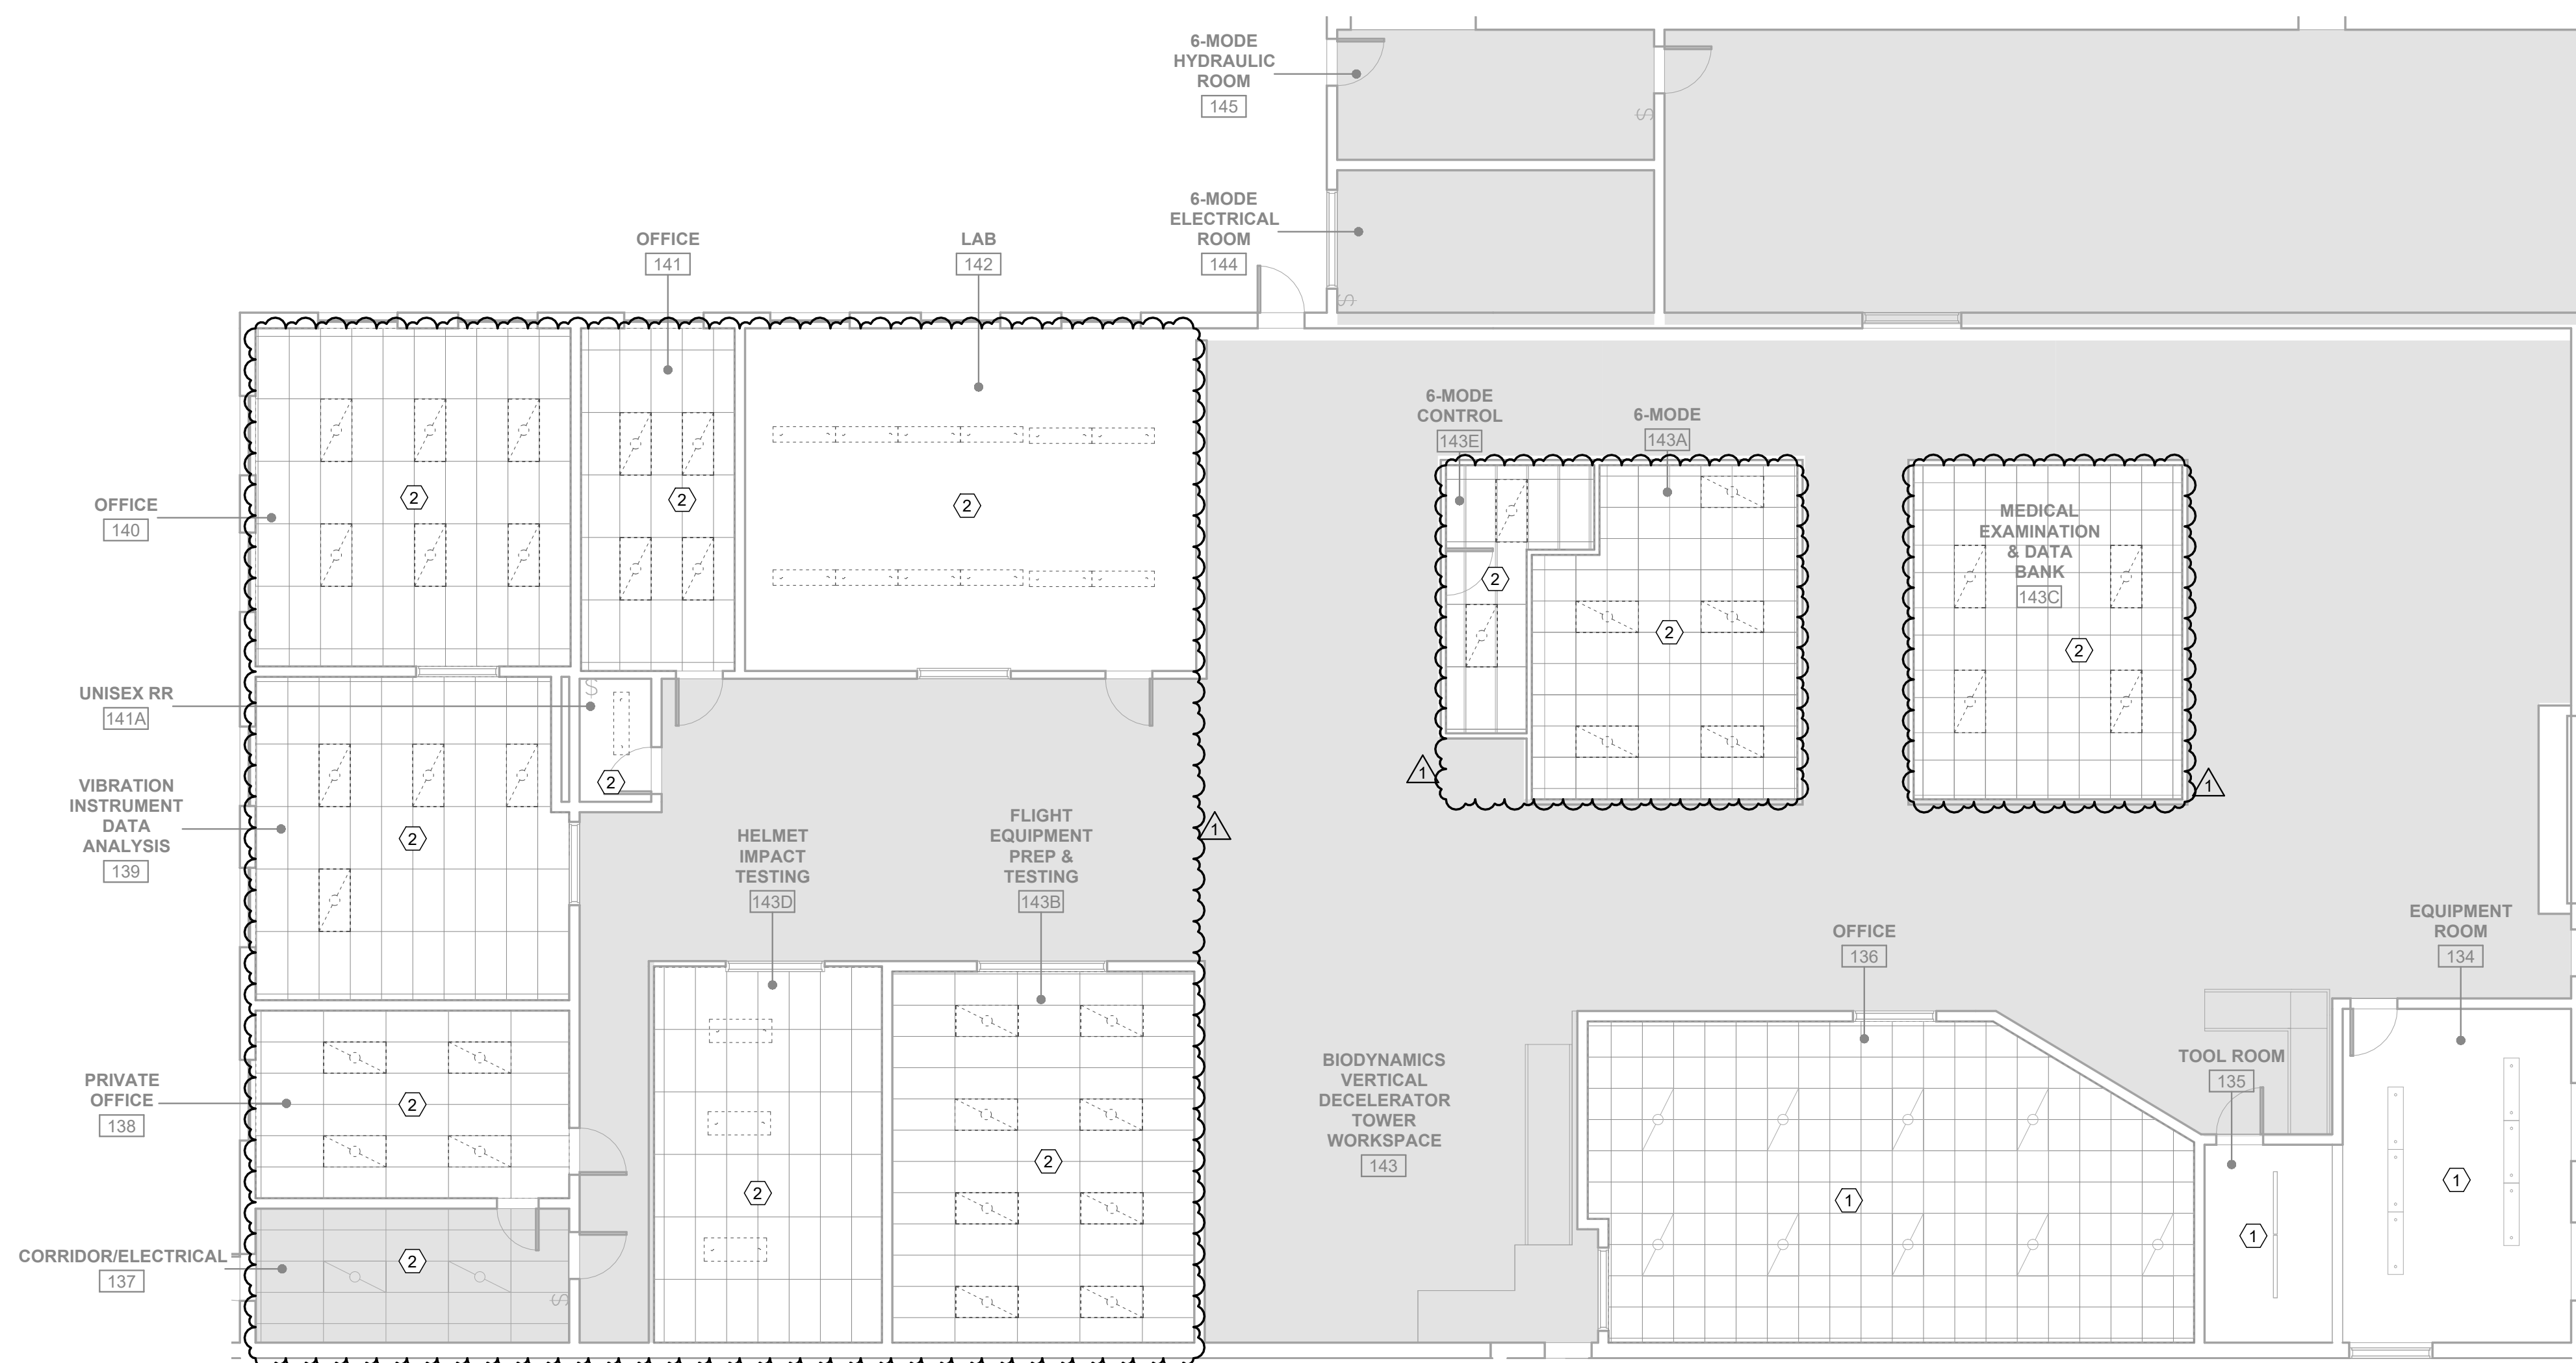

1 LEVEL 1 EAST- LIGHTING DEMO PLAN

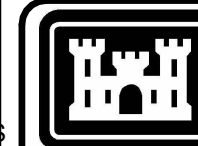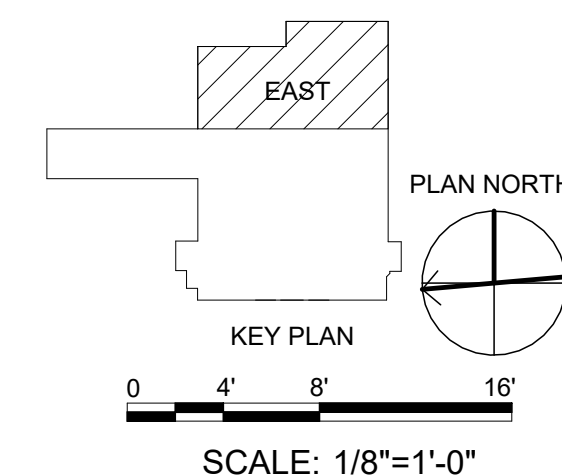

**US Army Corps
of Engineers ®**

[illegible]

US ARMY CORPS OF ENGINEERS LOUISVILLE DISTRICT 600 DR. MARTIN LUTHER KING, JR. PLACE, LOUISVILLE, KY, 40202-2239	DESIGNED BY:	ISSUE DATE:
	DRAWN BY:	SOLICITATION NO.:
	CHECKED BY:	CONTRACT NO.:
	SUBMITTED BY:	
	SIZE:	
ANSI D		


US ARMY CORPS OF ENGINEERS
LOUISVILLE DISTRICT
600 DR. MARTIN LUTHER KING, JR. PLACE



WRIGHT-PATTERSON AIR FORCE BASE, OHIO
HVAC & CONTROLS RENOVATION F/20824
F/2026
PROJECT NO. P2#: 513984, ZHTV231013
LEVEL 1 EAST - DEMO LIGHTING PLAN

SHEET ID:

ED212

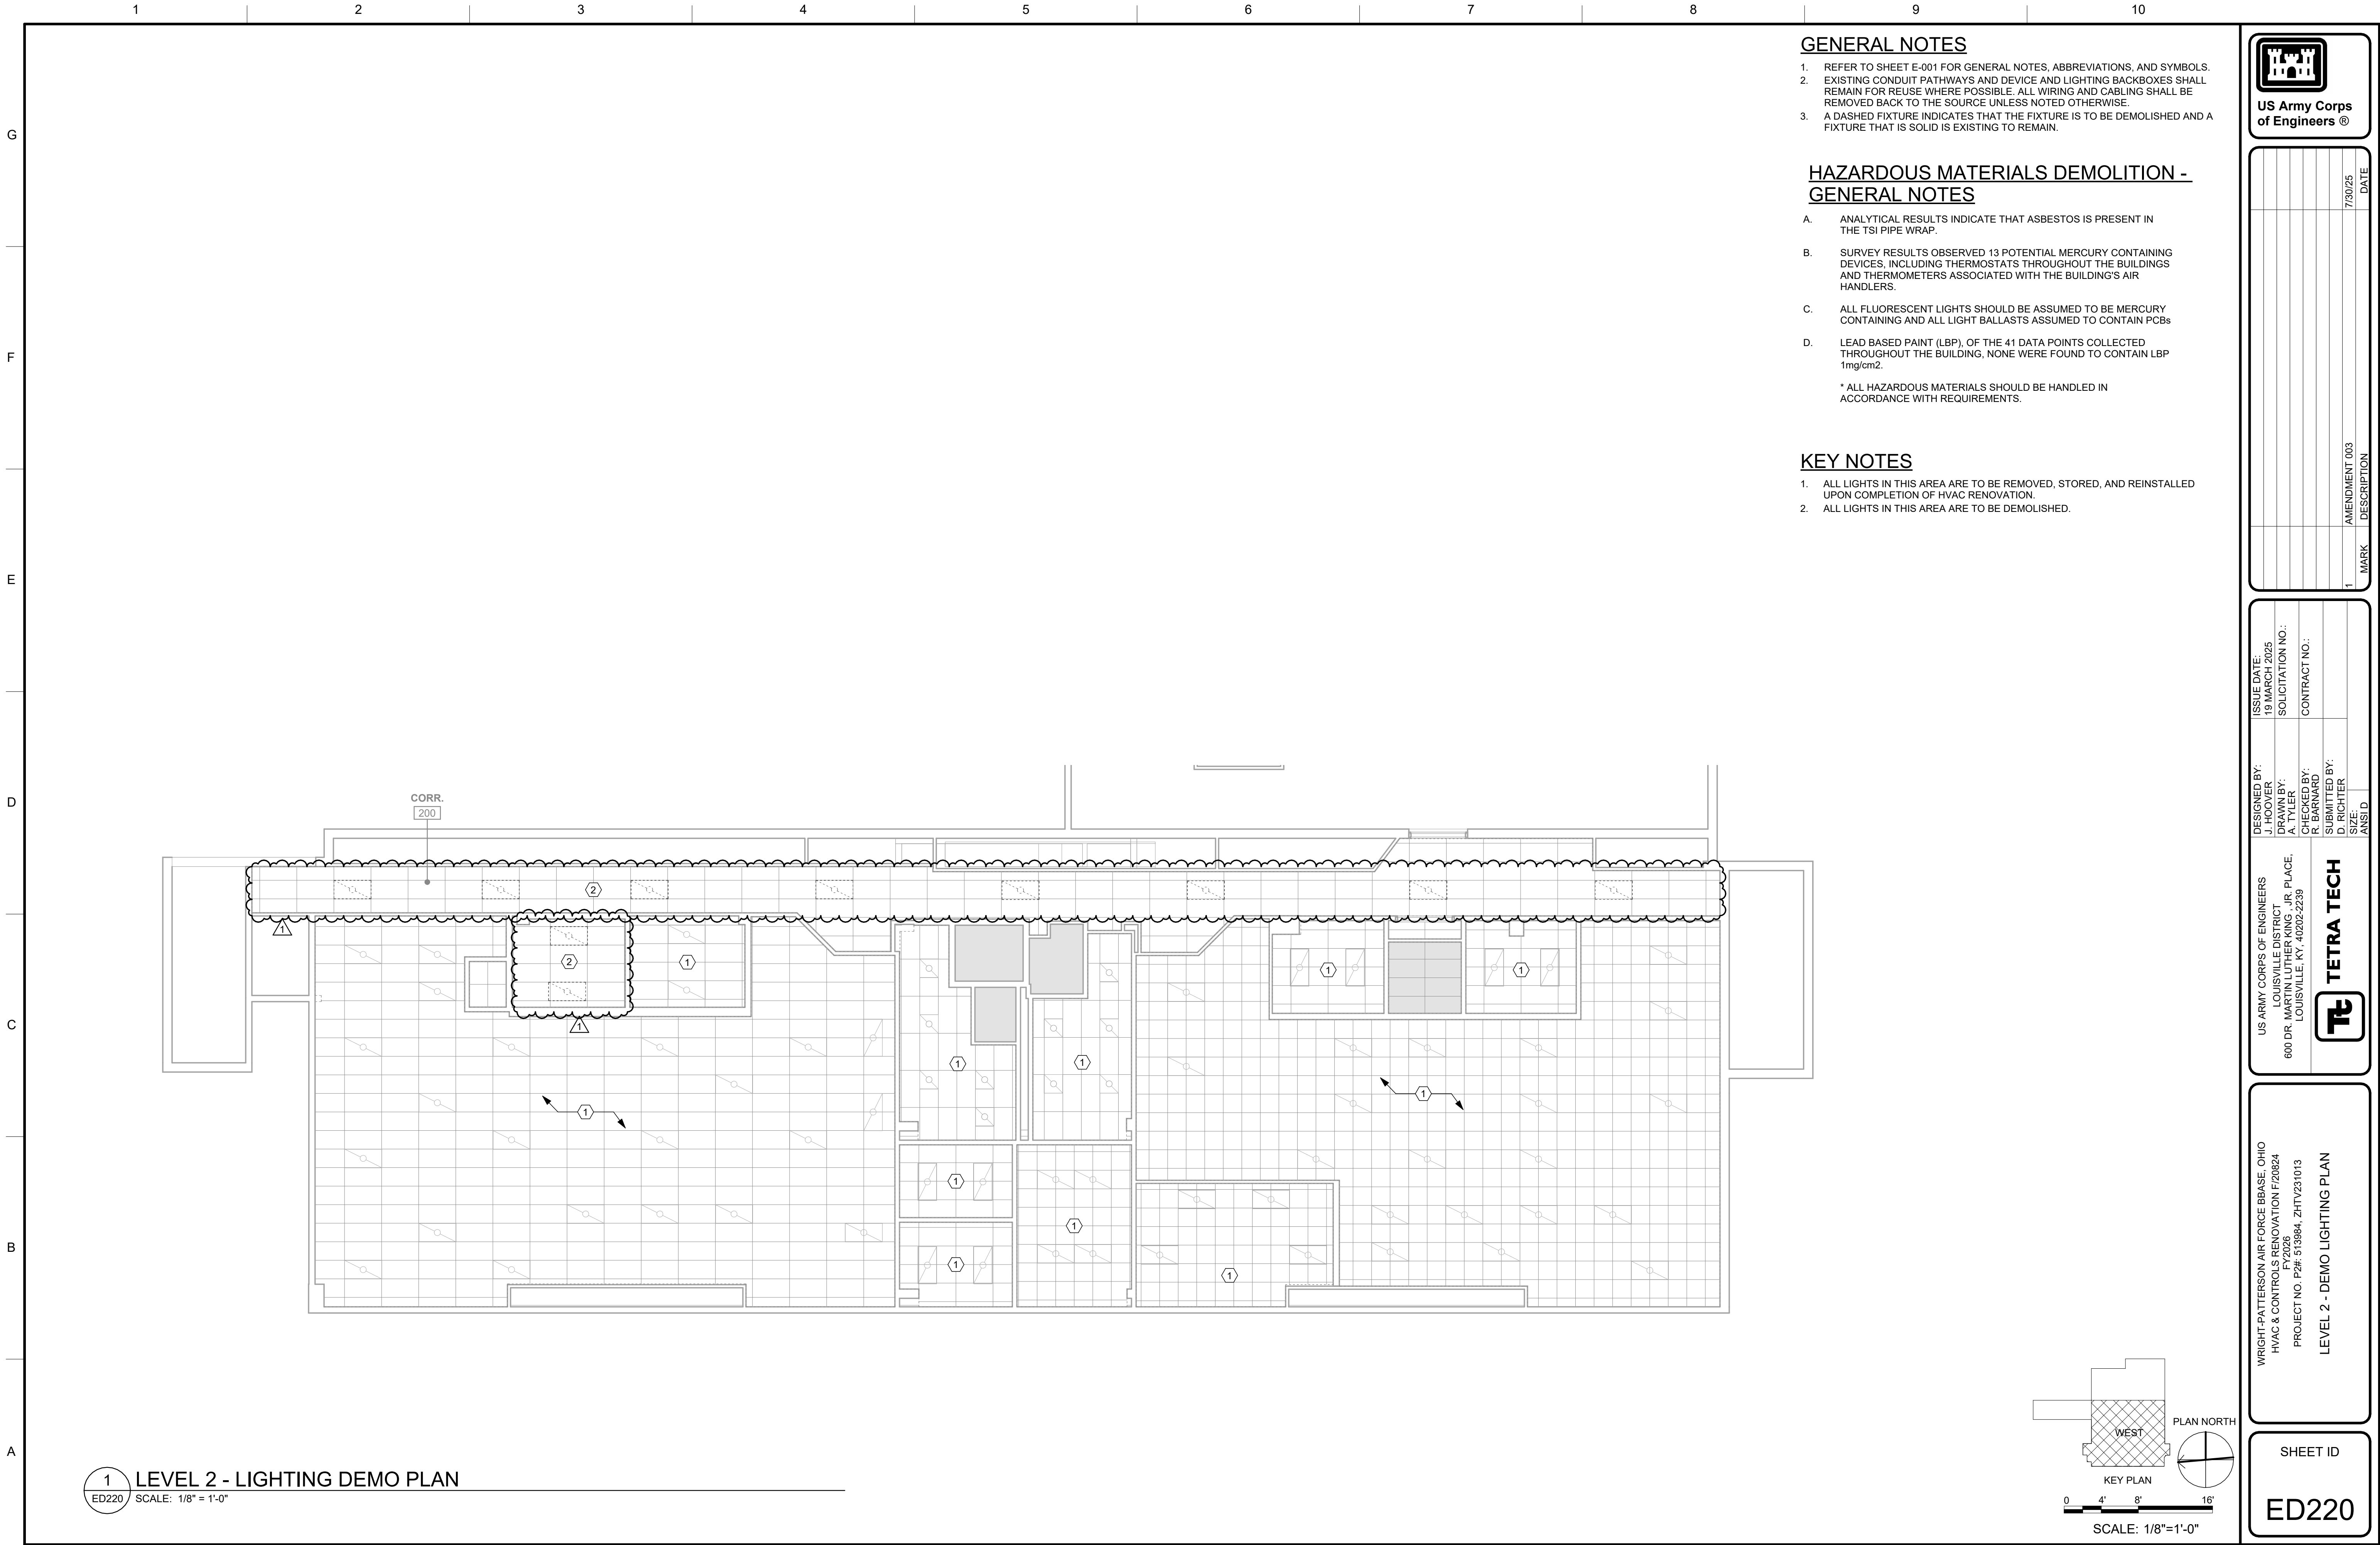


<

LIGHTING FIXTURE SCHEDULE

TYPE	MANUFACTURER	CATALOG NO.	VOLTAGE	WATTS	LAMP	MOUNTING	HEIGHT	REMARKS
A1E	LITHONIA	CPX 2X4 AL08 SWW7 M2	120 V	51 W	LED	RECESSED	PER CEILING	2X4 TROFFER
A1E	LITHONIA	CPX 2X4 AL08 SWW7 IM2 LBLP CP10 HE SD A	120 V	51 W	LED	RECESSED	PER CEILING	2X4 TROFFER WITH EMERGENCY BATTERY BACKUP
A2E	LITHONIA	CPX 2X4 AL08 SWW7 M2	120 V	37 W	LED	RECESSED	PER CEILING	2X4 TROFFER
A2E	LITHONIA	CPX 2X4 AL08 SWW7 IM2 LBLP CP10 HE SD A	120 V	37 W	LED	RECESSED	PER CEILING	2X4 TROFFER WITH EMERGENCY BATTERY BACKUP
A3	LITHONIA	CPX 2X4 AL08 SWW7 M2	120 V	29 W	LED	RECESSED	PER CEILING	2X4 TROFFER
A3E	LITHONIA	CPX 2X4 AL08 SWW7 IM2 LBLP CP10 HE SD A	120 V	29 W	LED	RECESSED	PER CEILING	2X4 TROFFER WITH EMERGENCY BATTERY BACKUP
B1	LITHONIA	ZL 1D-L48-3000LM-FST-MVOLT-35K-80CRI-BAA-WH-ZACVH M100	120 V	30 W	LED	PENDANT	PER CEILING HEIGHT	PENDANT FIXTURE
B1E	LITHONIA	ZL 1D-L48-3000LM-FST-MVOLT-35K-80CRI-E10W-BAA-WH-ZACVH M100	120 V	30 W	LED	PENDANT	PER CEILING HEIGHT	PENDANT FIXTURE WITH EMERGENCY BATTERY BACKUP
F	LITHONIA	LDN6-40/15-L06/AR-LSS-MVOLT-GZ10-BAA	120 V	38 W	LED	CEILING RECESSED	PER CEILING HEIGHT	DOWNLIGHT
FE	LITHONIA	LDN6-40/15-L06/AR-LSS-MVOLT-GZ10-E10WCP BAA	120 V	38 W	LED	CEILING RECESSED	PER CEILING HEIGHT	DOWNLIGHT WITH EMERGENCY BATTERY BACKUP
X	LITHONIA	LQM S W 3 R 120/277 EL N SD	<varies>	5 W	LED	WALL/CEILING SURFACE	8" - 0" / PER CEILING	LED EXIT SIGN WITH EMERGENCY BATTERY BACKUP

CABLE SCHEDULE (CU)

Label	CB Rating	# of Sets	Phase Conductors		Neutral Conductors		Grounding Conductors		Conduit	
			#	Size	#	Size	#	Size		
A	A20	20 A	1	#12	1	#12	1	#12	3/4"	
	A30	30 A	1	#10	1	#10	1	#10	3/4"	
	A40	40 A	1	#8	1	#8	1	#10	3/4"	
	A50	50 A	1	#6	1	#6	1	#10	1"	
	A60	60 A	1	#4	1	#4	1	#10	1"	
	A70	70 A	1	#4	1	#4	1	#8	1"	
	A80	80 A	1	#3	1	#3	1	#8	1-1/2"	
	A90	90 A	1	#2	1	#2	1	#8	1-1/2"	
	A100	100 A	1	#1	1	#1	1	#8	1-1/2"	
	A110	110 A	1	#1	1	#1	1	#6	1-1/2"	
	A125	125 A	1	#1	1	#1	1	#6	1-1/2"	
	A150	150 A	1	#1/0	1	#1/0	1	#6	1-1/2"	
	A175	175 A	1	#2/0	1	#2/0	1	#6	1-1/2"	
	A200	200 A	1	#3/0	1	#3/0	1	#6	2"	
	A225	225 A	1	#4/0	1	#4/0	1	#4	2"	
B	A250	250 A	1	250KCMIL	1	250KCMIL	1	#4	2"	
	A300	300 A	1	350KCMIL	1	350KCMIL	1	#4	2-1/2"	
	A350	350 A	1	500KCMIL	1	500KCMIL	1	#4	3"	
	A400	400 A	2	#3/0	1	#3/0	1	#3	2"	
	A450	450 A	2	#4/0	1	#4/0	1	#2	2"	
	B20	20 A	1	#12	0	N/A	1	#12	3/4"	
	B30	30 A	1	#10	0	N/A	1	#10	3/4"	
	B40	40 A	1	#8	0	N/A	1	#10	1"	
C	B50	50 A	1	#6	0	N/A	1	#10	1"	
	B60	60 A	1	#4	0	N/A	1	#10	1-1/2"	
	B70	70 A	1	#4	0	N/A	1	#8	1-1/2"	
	B80	80 A	1	#3	0	N/A	1	#8	1-1/2"	
	B90	90 A	1	#2	0	N/A	1	#8	1-1/2"	
	B100	100 A	1	#1	0	N/A	1	#8	1-1/2"	
	B110	110 A	1	#1	0	N/A	1	#6	1-1/2"	
	B125	125 A	1	#1/0	0	N/A	1	#6	1-1/2"	
	B150	150 A	1	#1/0	0	N/A	1	#6	2"	
	B175	175 A	1	#2/0	0	N/A	1	#6	2"	
	B200	200 A	1	#3/0	0	N/A	1	#6	2"	
	B225	225 A	1	#4/0	0	N/A	1	#4	2-1/2"	
	B250	250 A	1	250KCMIL	0	N/A	1	#4	2-1/2"	
	B300	300 A	1	350KCMIL	0	N/A	1	#4	3"	
	B350	350 A	1	500KCMIL	0	N/A	1	#3	3"	
	B400	400 A	2	#3/0	0	N/A	1	#3	2"	
	B450	450 A	2	#4/0	0	N/A	1	#2	2-1/2"	
	B500	500 A	2	250KCMIL	0	N/A	1	#2	2-1/2"	
B600	600 A	2	350KCMIL	0	N/A	1	#1	3"		
D	C20	20 A	1	#12	1	#12	1	#12	3/4"	
	C30	30 A	1	#10	1	#10	1	#10	3/4"	
	C40	40 A	1	#8	1	#8	1	#10	1"	
	C50	50 A	1	#6	1	#6	1	#10	1"	
	C60	60 A	1	#4	1	#4	1	#10	1-1/4"	
	C70	70 A	1	#4	1	#4	1	#8	1-1/4"	
	C80	80 A	1	#3	1	#3	1	#8	1-1/4"	
	C90	90 A	1	#2	1	#2	1	#8	1-1/2"	
	C100	100 A	1	#1	1	#1	1	#8	2"	
	C110	110 A	1	#1	1	#1	1	#6	2"	
	C125	125 A	1	#1	1	#1	1	#6	2"	
	C150	150 A	1	#1/0	1	#1/0	1	#6	2"	
	C175	175 A	1	#2/0	1	#2/0	1	#6	2"	
	C200	200 A	1	#3/0	1	#3/0	1	#6	2-1/2"	
	C225	225 A	1	#4/0	1	#4/0	1	#4	2-1/2"	
	C250	250 A	1	250KCMIL	1	250KCMIL	1	#4	2-1/2"	
	C300	300 A	1	350KCMIL	1	350KCMIL	1	#3	3-1/2"	
	C350	350 A	1	500KCMIL	1	500KCMIL	1	#3	3-1/2"	
	C400	400 A	2	#3/0	1	#3/0	1	#3	2-1/2"	
	C450	450 A	2	#4/0	1	#4/0	1	#2	2-1/2"	
E	C500	500 A	2	250KCMIL	1	250KCMIL	1	#2	3"	
	C600	600 A	2	350KCMIL	1	350KCMIL	1	#1	3"	
	C800	800 A	4	300KCMIL	1	300KCMIL	1	#10	3"	
	C1000	1,000 A	4	250KCMIL	1	250KCMIL	1	#2/0	3"	
	C1200	1,200 A	4	350KCMIL	1	350KCMIL	1	#3/0	3-1/2"	
	C1600	1,600 A	5	500KCMIL	1	500KCMIL	1	#4/0	4"	
	C2000	2,000 A	6	500KCMIL	1	500KCMIL	1	250KCMIL	4"	
	C2500	2,500 A	7	500KCMIL	1	500KCMIL	1	350KCMIL	4"	
	C3000	3,000 A	8	500KCMIL	1	500KCMIL	1	500KCMIL	4"	
	C4000	4,000 A	11	350KCMIL	1	500KCMIL	1	500KCMIL	4"	
	F	C20N	20 A	1	#10	1	#8	1	#10	1"
		C30N	30 A	1	#6	1	#3	1	#10	1-1/4"
		C40N	40 A	1	#6	1	#1	1	#10	1-1/4"
		C50N	50 A	1	#4	1	#1	1	#8	1-1/2"
		C60N	60 A	1	#3	1	#1/0	1	#8	1-1/2"
		C70N	70 A	1	#2	1	#2/0	1	#8	2"
		C80N	80 A	1	#1	1	#3/0	1	#8	2"
		C90N	90 A	1	#1	1	#4/0	1	#6	2"
		C100N	100 A	1	#1	1	250KCMIL	1	#6	2"
		C110N	110 A	1	#1/0	2	#1/0	1	#6	2-1/2"
C125N		125 A	1	#2/0	2	#2/0	1	#6	2-1/2"	
C150N		150 A	1	#3/0	2	#3/0	1	#6	2-1/2"	
C175N		175 A	1	#4/0	2	#4/0	1	#4	3"	
C200N		200 A	1	250KCMIL	2	250KCMIL	1	#4	3"	
C225N		225 A	1	300KCMIL	2	300KCMIL	1	#4	3-1/2"	
G	C250N	250 A	1	500KCMIL	2	500KCMIL	1	#3	4"	
	C300N	300 A	1	500KCMIL	2	500KCMIL	1	#3	4"	
	C350N	350 A	2	#4/0	2	#4/0	1	#2	3"	
	C400N	400 A	2	250KCMIL	2	250KCMIL	1	#2	3"	
	C450N	450 A	2	300KCMIL	2	300KCMIL	1	#1	3-1/2"	
	C500N	500 A	2	300KCMIL	2	500KCMIL	1	#1/0	4"	
	C600N	600 A	2	500KCMIL	2	500KCMIL	1	#1/0	4"	
	C800N	800 A	4	250KCMIL	2	250KCMIL	1	#2/0	3"	
	C1000N	1,000 A	4	500KCMIL	2	500KCMIL	1	#4/0	4"	
	C1200N	1,200 A	4	500KCMIL	2	500KCMIL	1	#4/0	4"	
	C1600N	1,600 A	6	500KCMIL	2	500KCMIL	1	250KCMIL	4"	
	C2000N	2,000 A	7	500KCMIL	2	500KCMIL	1	350KCMIL	4"	
	C2500N	2,500 A	9	500KCMIL	2	500KCMIL	1	500KCMIL	4"	
	C3000N	3,000 A	10	500KCMIL	2	500KCMIL	1	500KCMIL	4"	
	C4000N	4,000 A	11	350KCMIL	2	750KCMIL	1	750KCMIL	5"	
H	C2000S	2,000 A	6	500KCMIL	1	500KCMIL	0	N/A	4"	

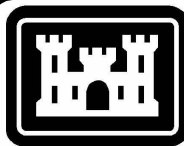

**US Army Corps
of Engineers ®**

[illegible]

 TETRA TECH		DESIGNED BY: US ARMY CORPS OF ENGINEERS		ISSUE DATE: 9 MARCH 2025	
LOUISVILLE DISTRICT 800 DR. MARTIN LUTHER KING LOUISVILLE, KY 40205-2239		DRAWN BY: A. TYLER		SOLICITATION NO.:	
		CHECKED BY: R. BARNARD		CONTRACT NO.:	
		SUBMITTED BY:			
		SIZE:		INCHES:	

WRIGHT-PATTERSON AIR FORCE BASE, OHIO
HVAC & CONTROLS RENOVATION F/20824
FY2026
PROJECT NO. P2#: 513984, ZHTV231013

SHEET ID

E-602

GENERAL NOTES

1. REFER TO SHEET E-001 FOR GENERAL NOTES, ABBREVIATIONS, AND SYMBOLS.
2. ALL NEW LOADS ARE SIGNIFIED BY DARKER TEXT IN THE PANEL SCHEDULES. ALL EXISTING LOADS ARE GRAYED OUT.



**US Army Corps
of Engineers ®**

[illegible]

US ARMY CORPS OF ENGINEERS LOUISVILLE DISTRICT 6000 DR. MARTIN LUTHER KING, JR. PLACE, LOUISVILLE, KY. 40202-2239	DESIGNED BY: J. HOOVER	ISSUE DATE: 19 MARCH 2025
	DRAWN BY: A. TYLER	SOLICITATION NO.:
	CHECKED BY: R. BARNARD	CONTRACT NO.:
	SUBMITTED BY: D. RICHTER	

RIGHT-PATTERSON AIR FORCE BBASE, OHIO
HVAC & CONTROLS RENOVATION F/20824
FY2026
PROJECT NO. P2#: 513984, ZHTV231013
ELECTRICAL PANEL SCHEDULES

SHEET ID

E-604

W912QR25B0053 Plans-0003

CERTIFIED FINAL