




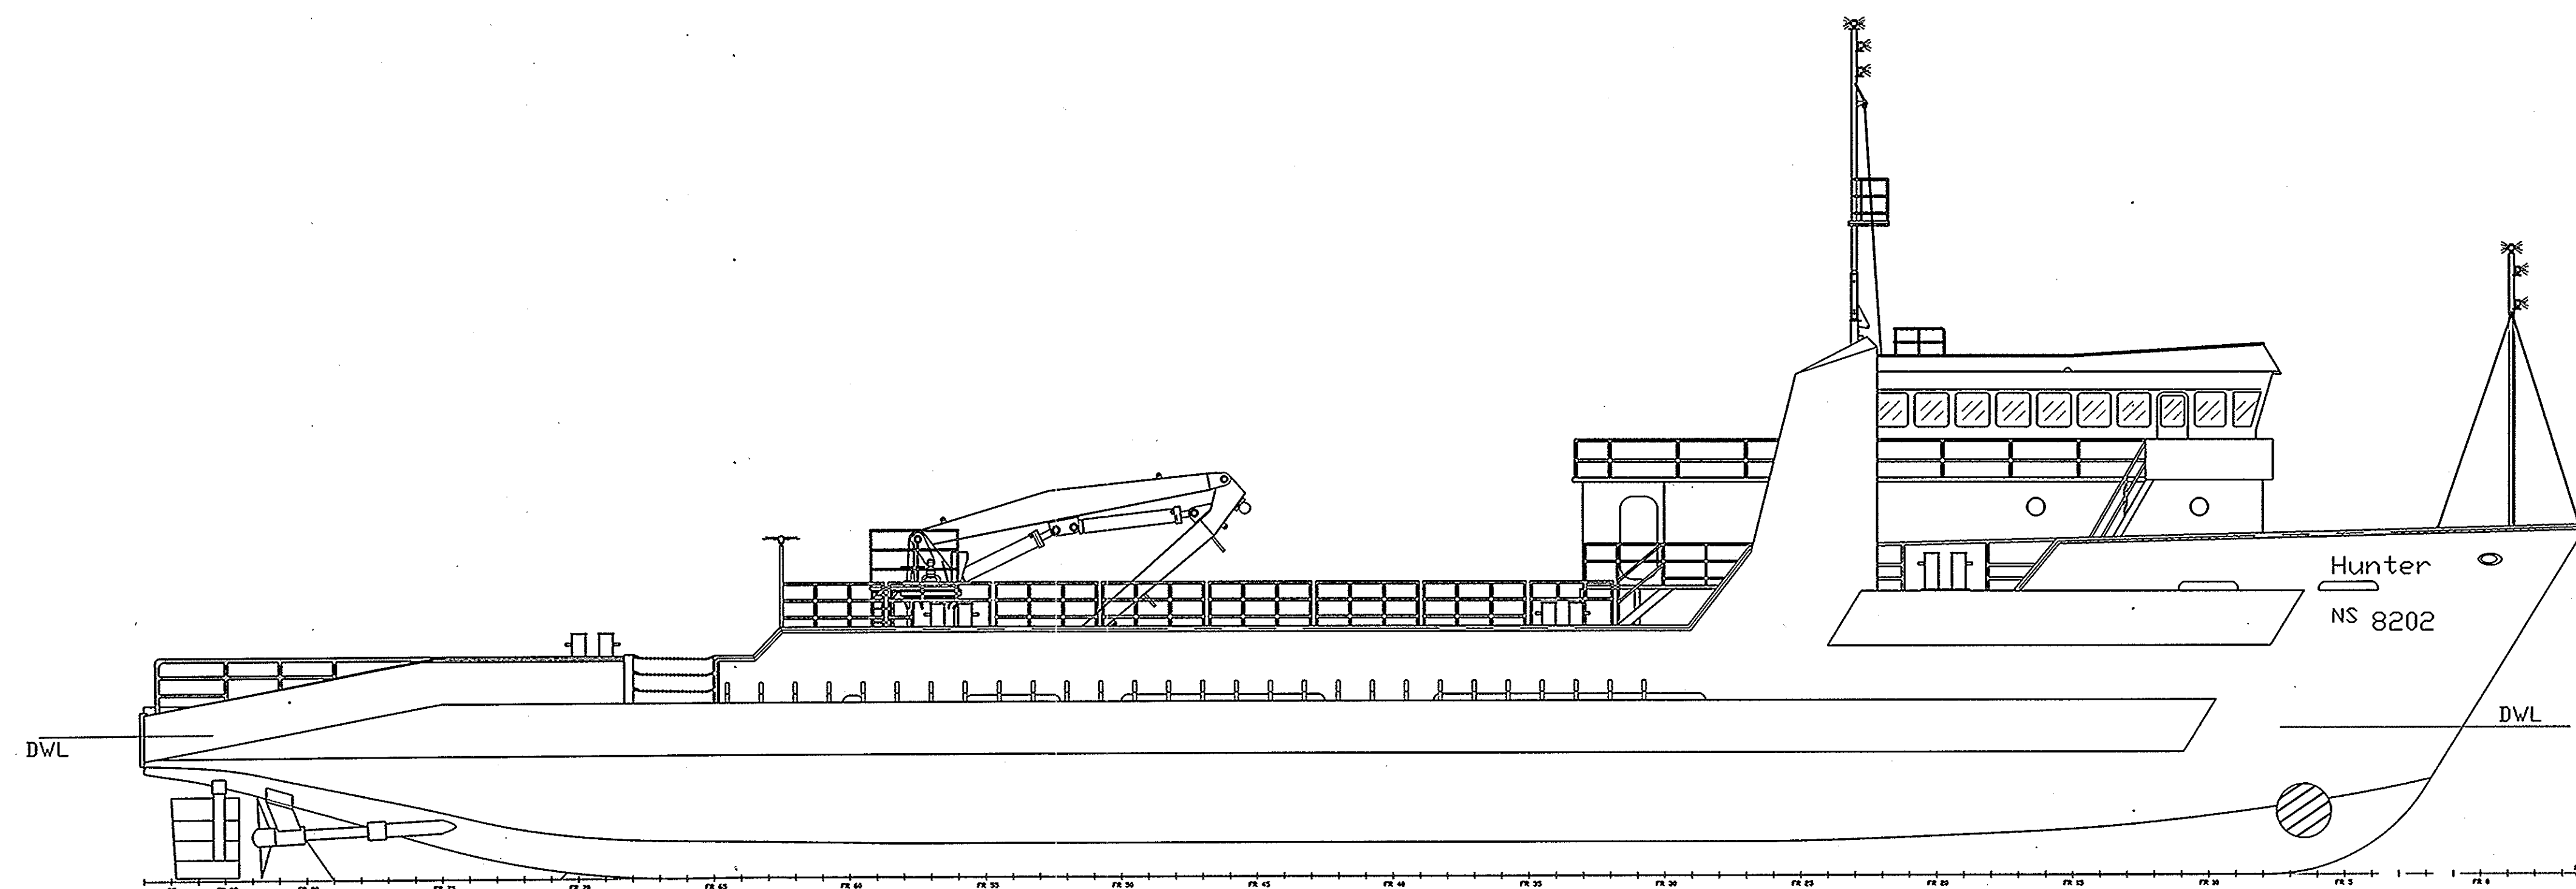

STBD PROFILE

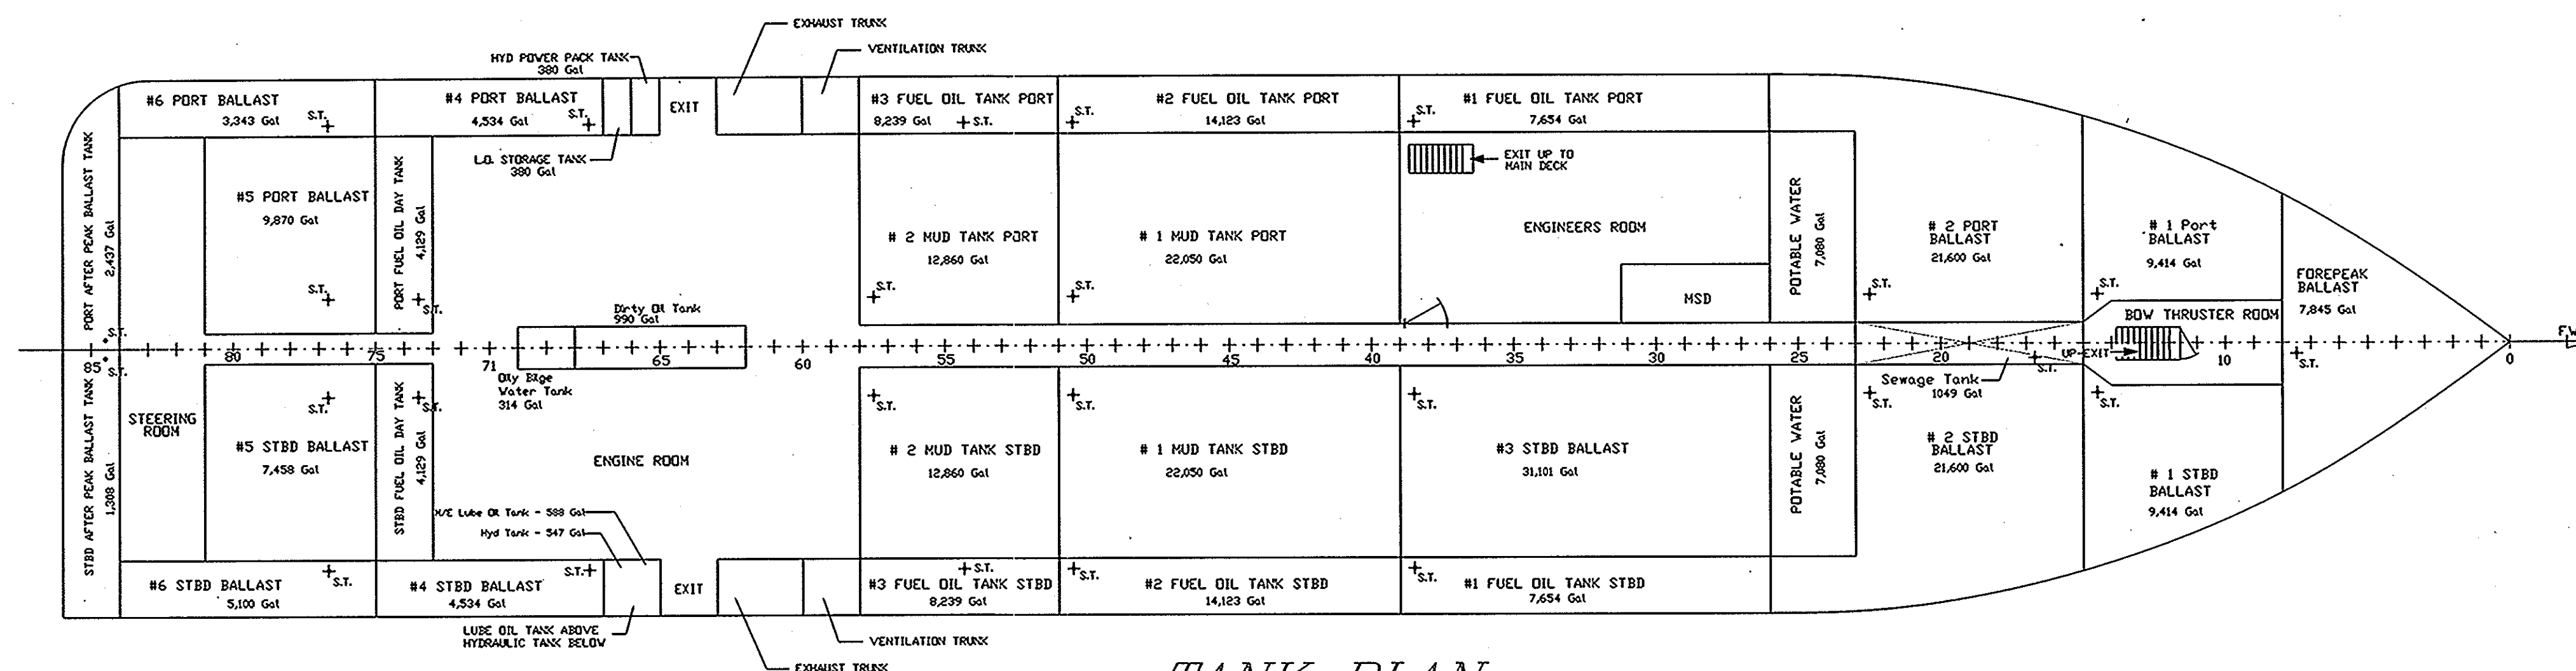

TANK PLAN

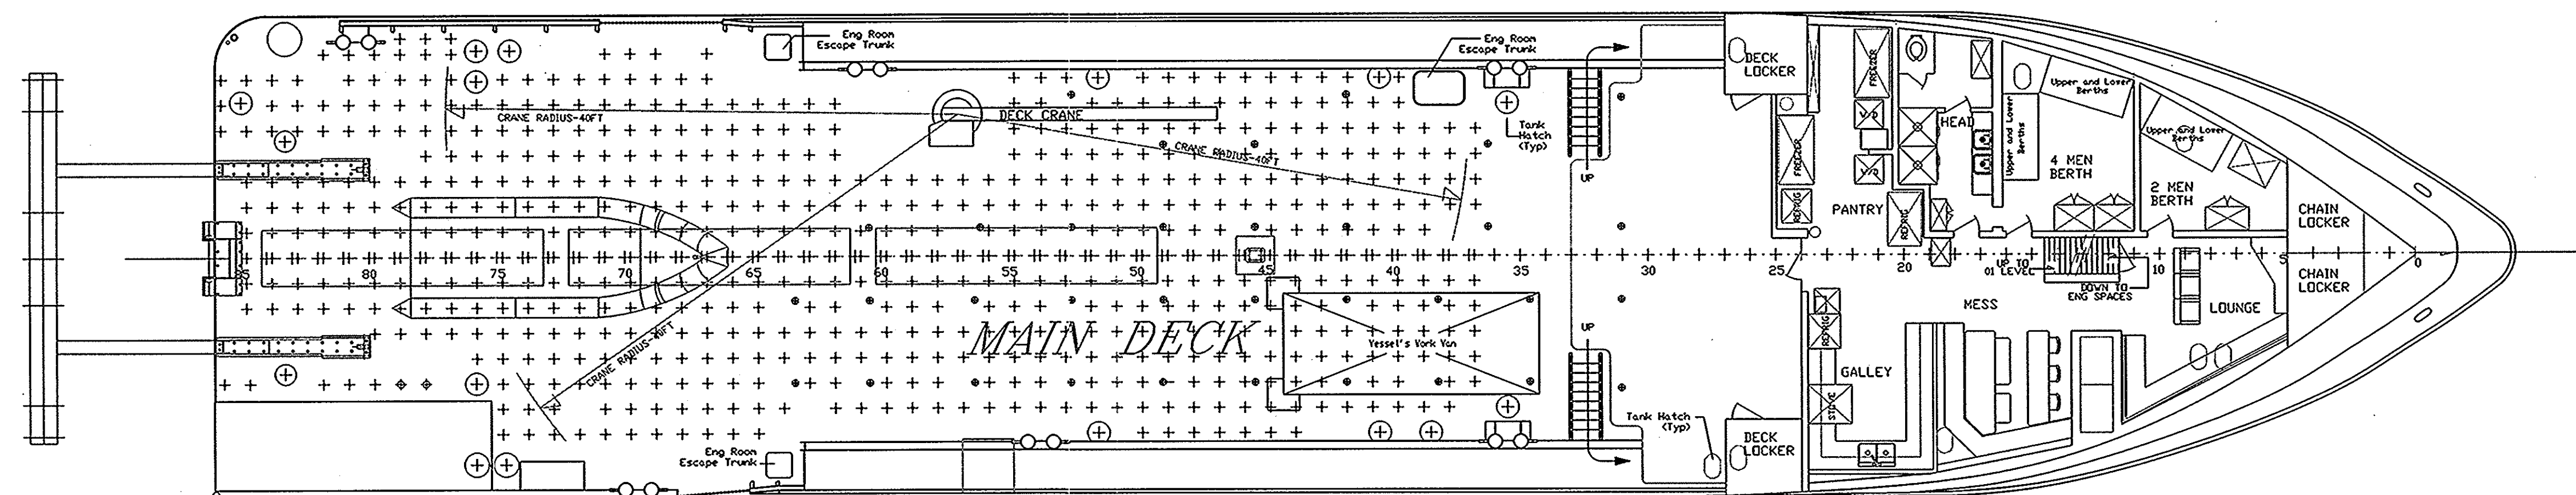


MAIN DECK PLAN


PARTICULARS

Builder - Quality Shipbuilders Inc, 1981 Hull # - 116
 Converted to T-IV 1991
 Dimensions - 179'-6" x 38' x 13'
 Summer Draft - 10' 11"
 Displacement - 619.79 LT
 Fuel Capacity - 68,290 Gallons
 Main Power - 2 x Caterpillar D-399, 1090 hp/ea
 Aux Power - 2 x 170 KW Caterpillar Generator, 3306

Offical Number - 642262
 ABS ID - 8129612
 Loadline - ABS, 2009

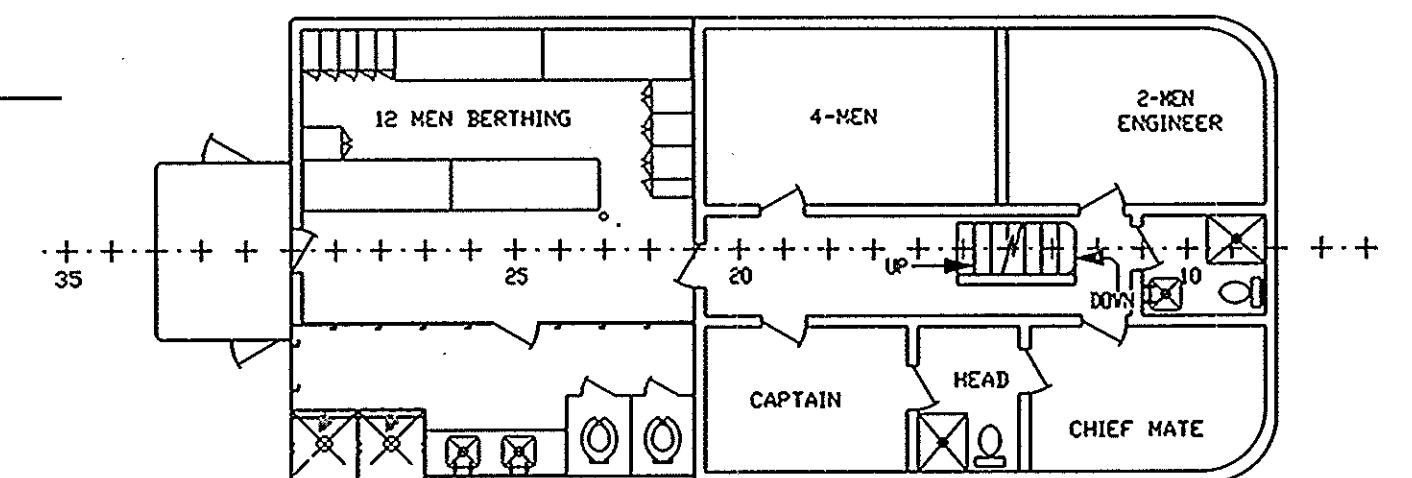

01 LEVEL

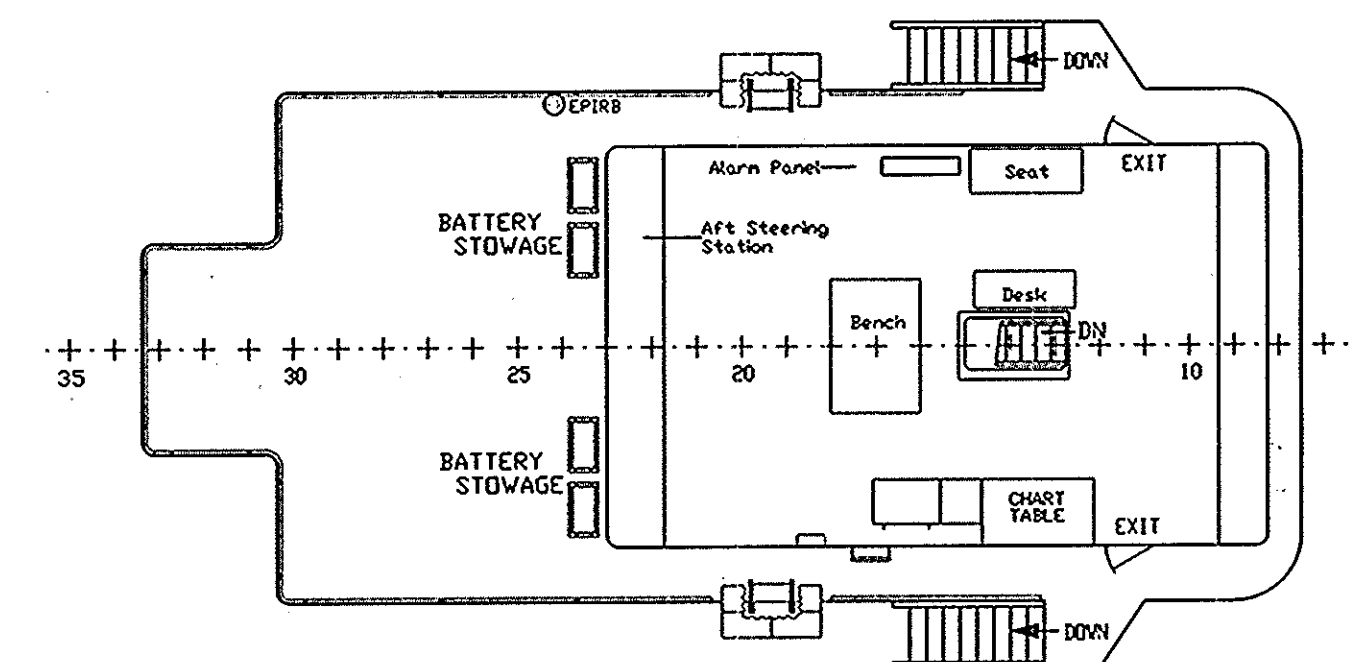

WHEELHOUSE

REVISIONS		
DATE	BY	Notes / Details
--	--	_____
--	--	_____
--	--	_____

TOLERANCES UNLESS OTHERWISE SPECIFIED		 SEAWARD SERVICES, INC. 1850 SE 17th St, Suite 300, Fort Lauderdale FL 33316	
FRANCHISE ANGLES 8 PLACE DECIMALS 3 PLACE DECIMAL		N/S HUNTER - General Arrangement	
DRAWN G. Wolner CHECKED _____ EXCOR _____ APPROVED _____		SIZE 202-GA-106	DRAWING NO. REV. -
SCALE 1/8" = 1' DATE 11-11 SHEET 1 OF 1			