

UNITED STATES DEPARTMENT OF THE INTERIOR
FISH AND WILDLIFE SERVICE
NORTHEAST ANADROMOUS FISH RESEARCH LABORATORY
WESTERN MASSACHUSETTS ELECTRIC COMPANY TRACTS
(10,R,M,M-1)
25.64 ACRES


Town of Montague, Franklin County, Massachusetts
Scale 0 200 400 600 800 Feet

ACREAGE		
TRACT	FEE	R.O.W.
10	20.00	-
10R	-	11.21
10M	-	5.16
10M-I	-	0.48
TOTAL	20.00	16.85

TRACT 10		
COR	BEARINGS	FEET
194	S16°54'W	347.44
193	S04°16'W	175.00
211	S04°16'W	507.39
205	S04°16'W	100.47
204	S04°16'W	30.00
199	S01°43'W	101.02
197	S02°24'E	103.59
203	S07°36'W	127.09
174	N35°20'W	100.00
172	N59°15'W	193.68
171	N62°02'W	166.63
170	N71°43'W	311.79
169	N08°56'W	111.66
168	N33°51'E	184.74
167	N15°36'W	134.74
166	N06°52'E	202.01
165	N45°48'E	183.37
164	N49°58'E	407.88
163	N57°47'E	283.42
162	S54°52'E	241.69
194		

TRACT 10R		
COR	BEARING	FEET
211	N04°16'E	175.00
193	N16°54'E	347.44
194	N54°52'W	45.49
235	N45°39'E	420.45
237	N58°25'E	1,402.79
238	N71°09'E	270.50
242	N88°51'E	392.50
221	N40°16'E	1230.10
220	S49°44'E	60.00
219	N40°16'E	60.00
218	S49°46'E	134.31
222	Southwesterly along the meanders of the normal operating level of the Power Canal.	
		42002
223	N83°44'W	52.02
211		

* Proposed 30' easement
15' each side of &
except as noted from
MP 1036 to MP 1037

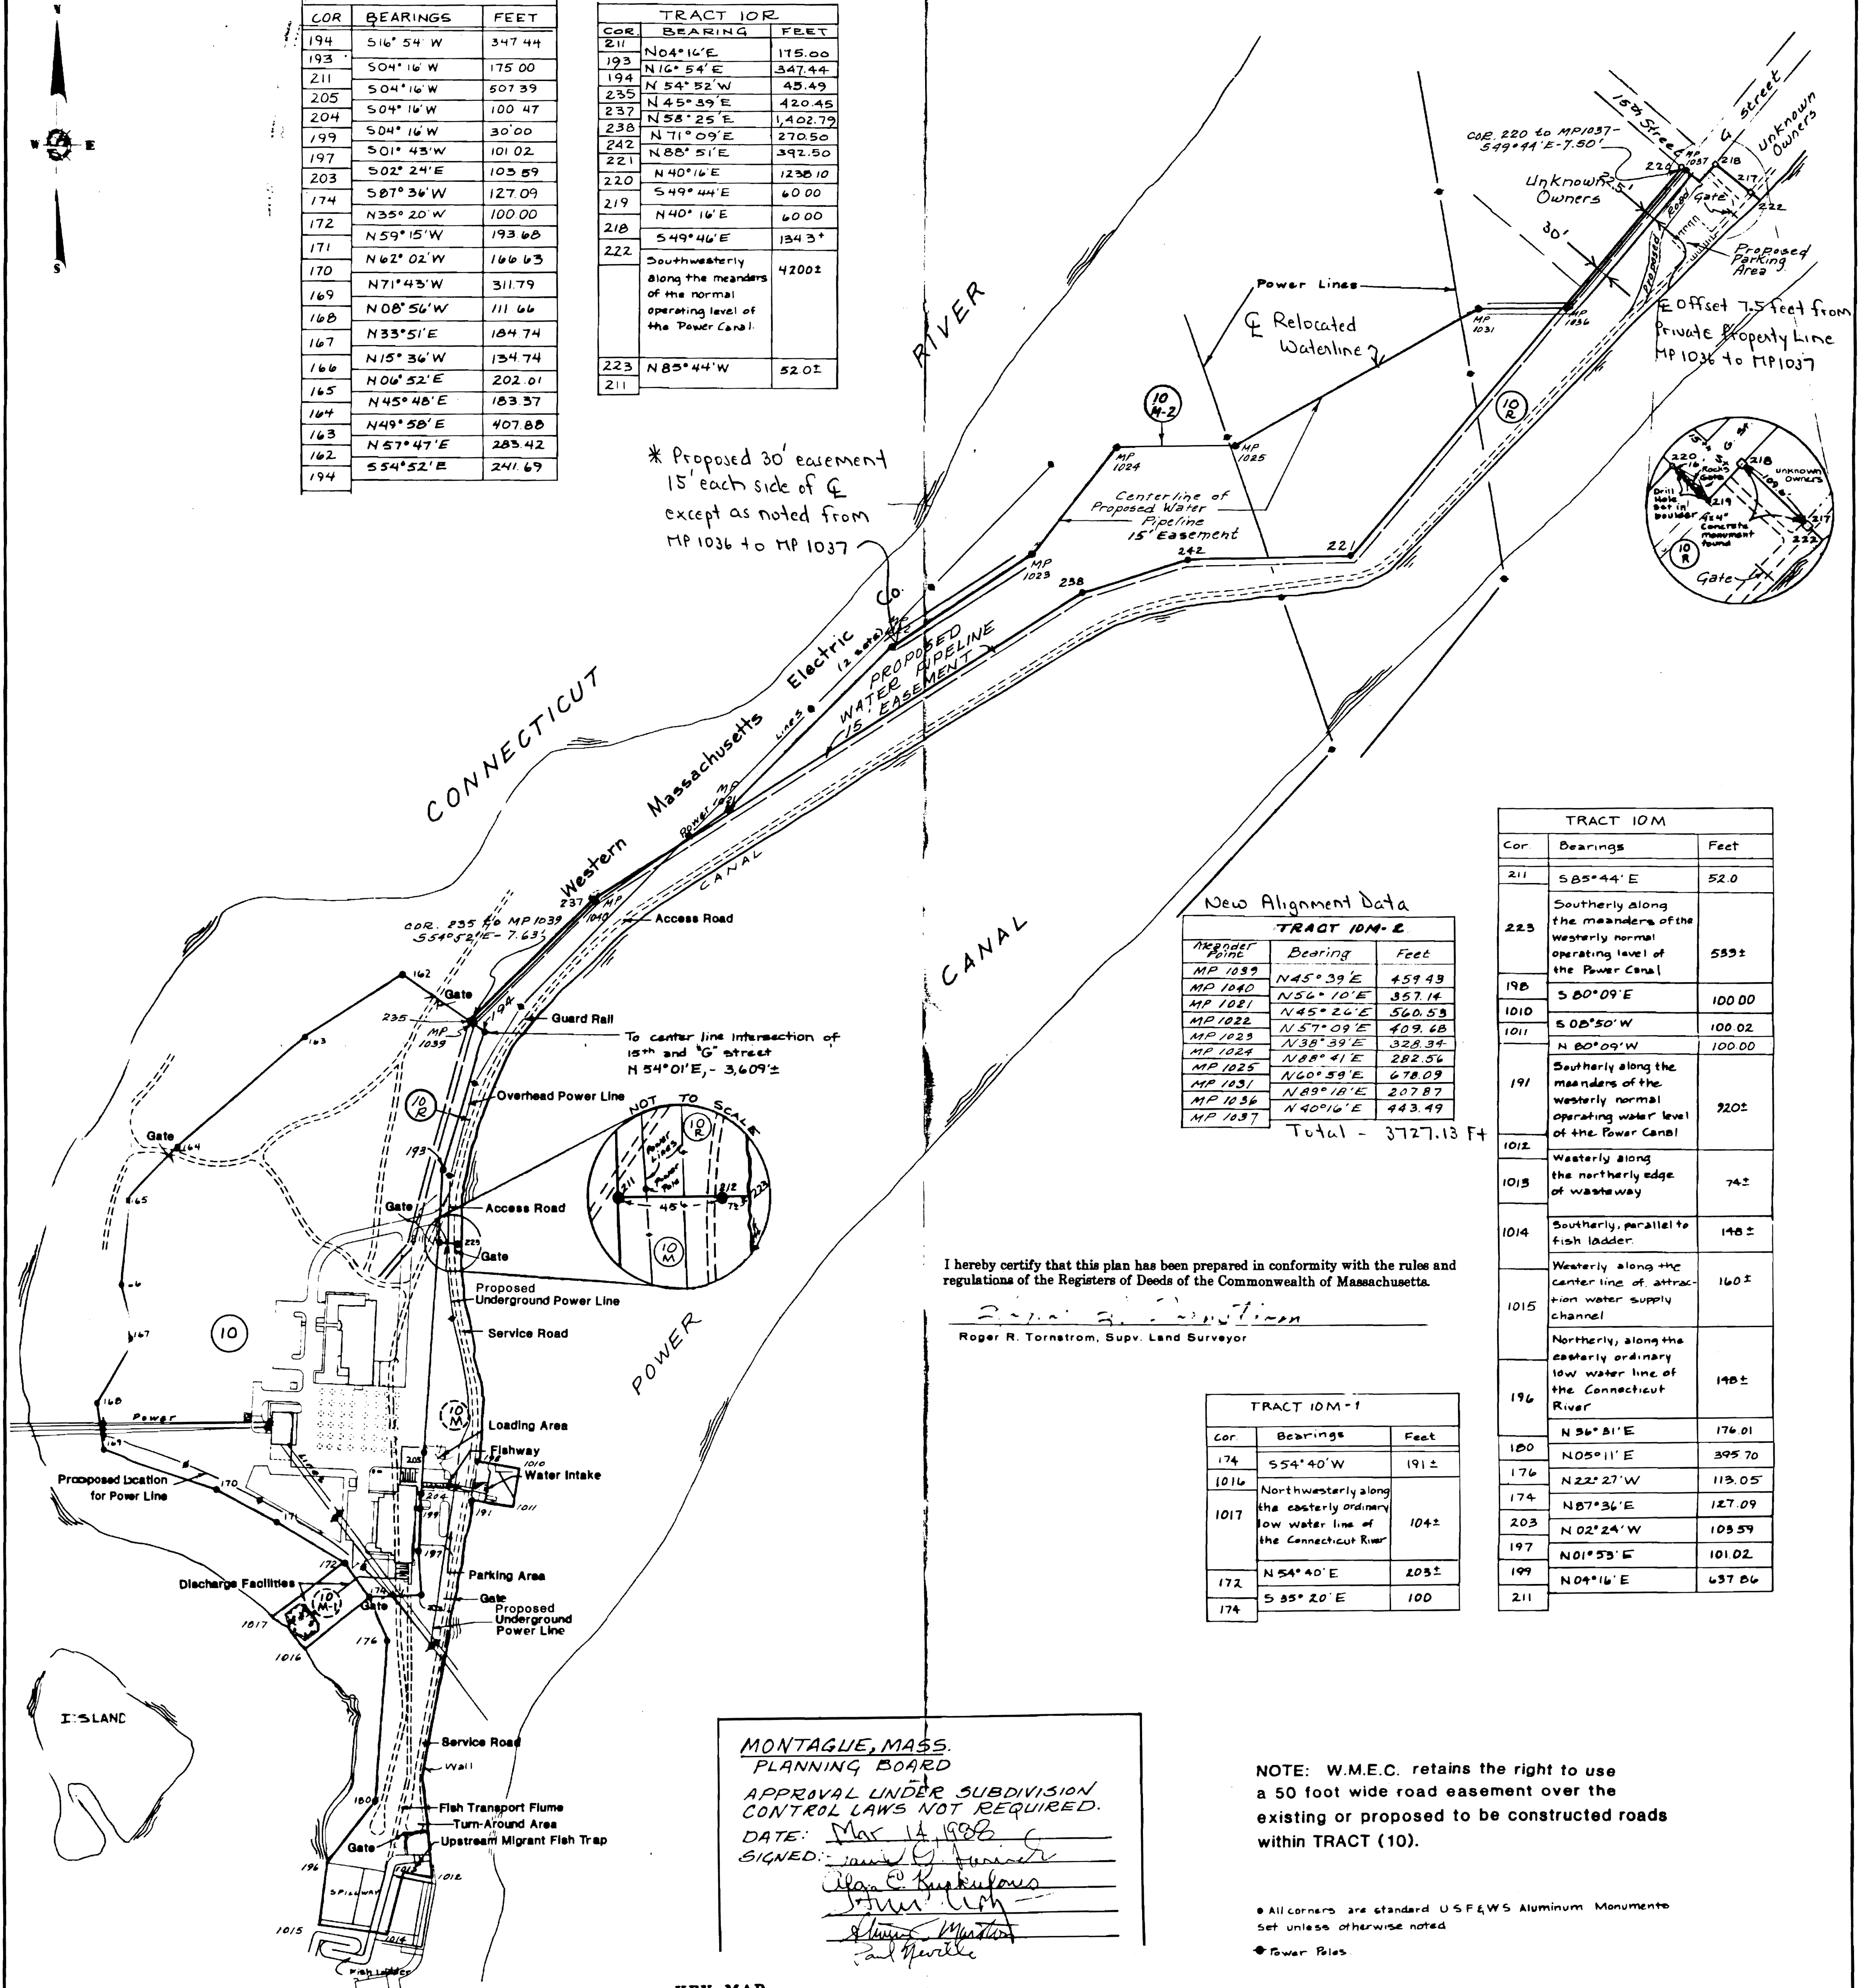

New Alignment Data		
TRACT 10M-E		
MP	Bearing	Feet
MP 1039	N45°39'E	459.49
MP 1040	N56°10'E	357.14
MP 1021	N45°24'E	560.53
MP 1022	N57°09'E	409.68
MP 1023	N38°39'E	328.34
MP 1024	N88°41'E	282.56
MP 1025	N60°59'E	678.09
MP 1031	N89°18'E	207.87
MP 1036	N40°16'E	443.49
MP 1037		
Total = 3727.13 Ft		

TRACT 10M		
Cor	Bearings	Feet
211	S85°44'E	52.0
223	Southernly along the meanders of the westerly normal operating level of the Power Canal	
		5592
198	S80°09'E	100.00
1010	S80°09'E	100.00
1011	N80°09'W	100.00
191	Southernly along the meanders of the westerly normal operating water level of the Power Canal	
		2202
1012	Westerly along the northern edge of washway	
		742
1013	Southernly, parallel to fish ladder	
		148±
1014	Westerly along the center line of attraction water supply channel	
		160±
1015	Northernly, along the easterly ordinary low water line of the Connecticut River	
		148±
196	N36°31'E	176.01
180	N05°11'E	395.70
176	N22°27'W	113.05
174	N87°36'E	127.09
203	N02°24'W	103.59
197	N01°53'E	101.02
199	N04°16'E	637.86
211		

TRACT 10M-I		
Cor	Bearings	Feet
174	S54°40'W	191±
1016	Northwesterly along the easterly ordinary low water line of the Connecticut River	
		104±
1017	N54°40'E	203±
172	S35°20'E	100
174		

I hereby certify that this plan has been prepared in conformity with the rules and regulations of the Registers of Deeds of the Commonwealth of Massachusetts.

Roger R. Tornstrom, Supv. Land Surveyor

MONTAGUE, MASS.
PLANNING BOARD
APPROVAL UNDER SUBDIVISION
CONTROL LAWS NOT REQUIRED.
DATE: Mar 14, 1988
SIGNED: [Signatures]

NOTE: W.M.E.C. retains the right to use a 50 foot wide road easement over the existing or proposed to be constructed roads within TRACT (10).

• All corners are standard U.S.F.W.S. Aluminum Monuments set unless otherwise noted.
• Power Poles.

THIS MAP was compiled from surveys of the United States Fish and Wildlife Service made from May 20, 1986 to December 4, 1986 and from records in the files thereof.

Roger R. Tornstrom
December 12, 1986
Roger R. Tornstrom, Supv. Land Surveyor
Office of Realty

NOTE: The improvements as shown on this plat are an illustration of proposed engineering drawings and may not represent the exact location, size, detail and final design after construction.