



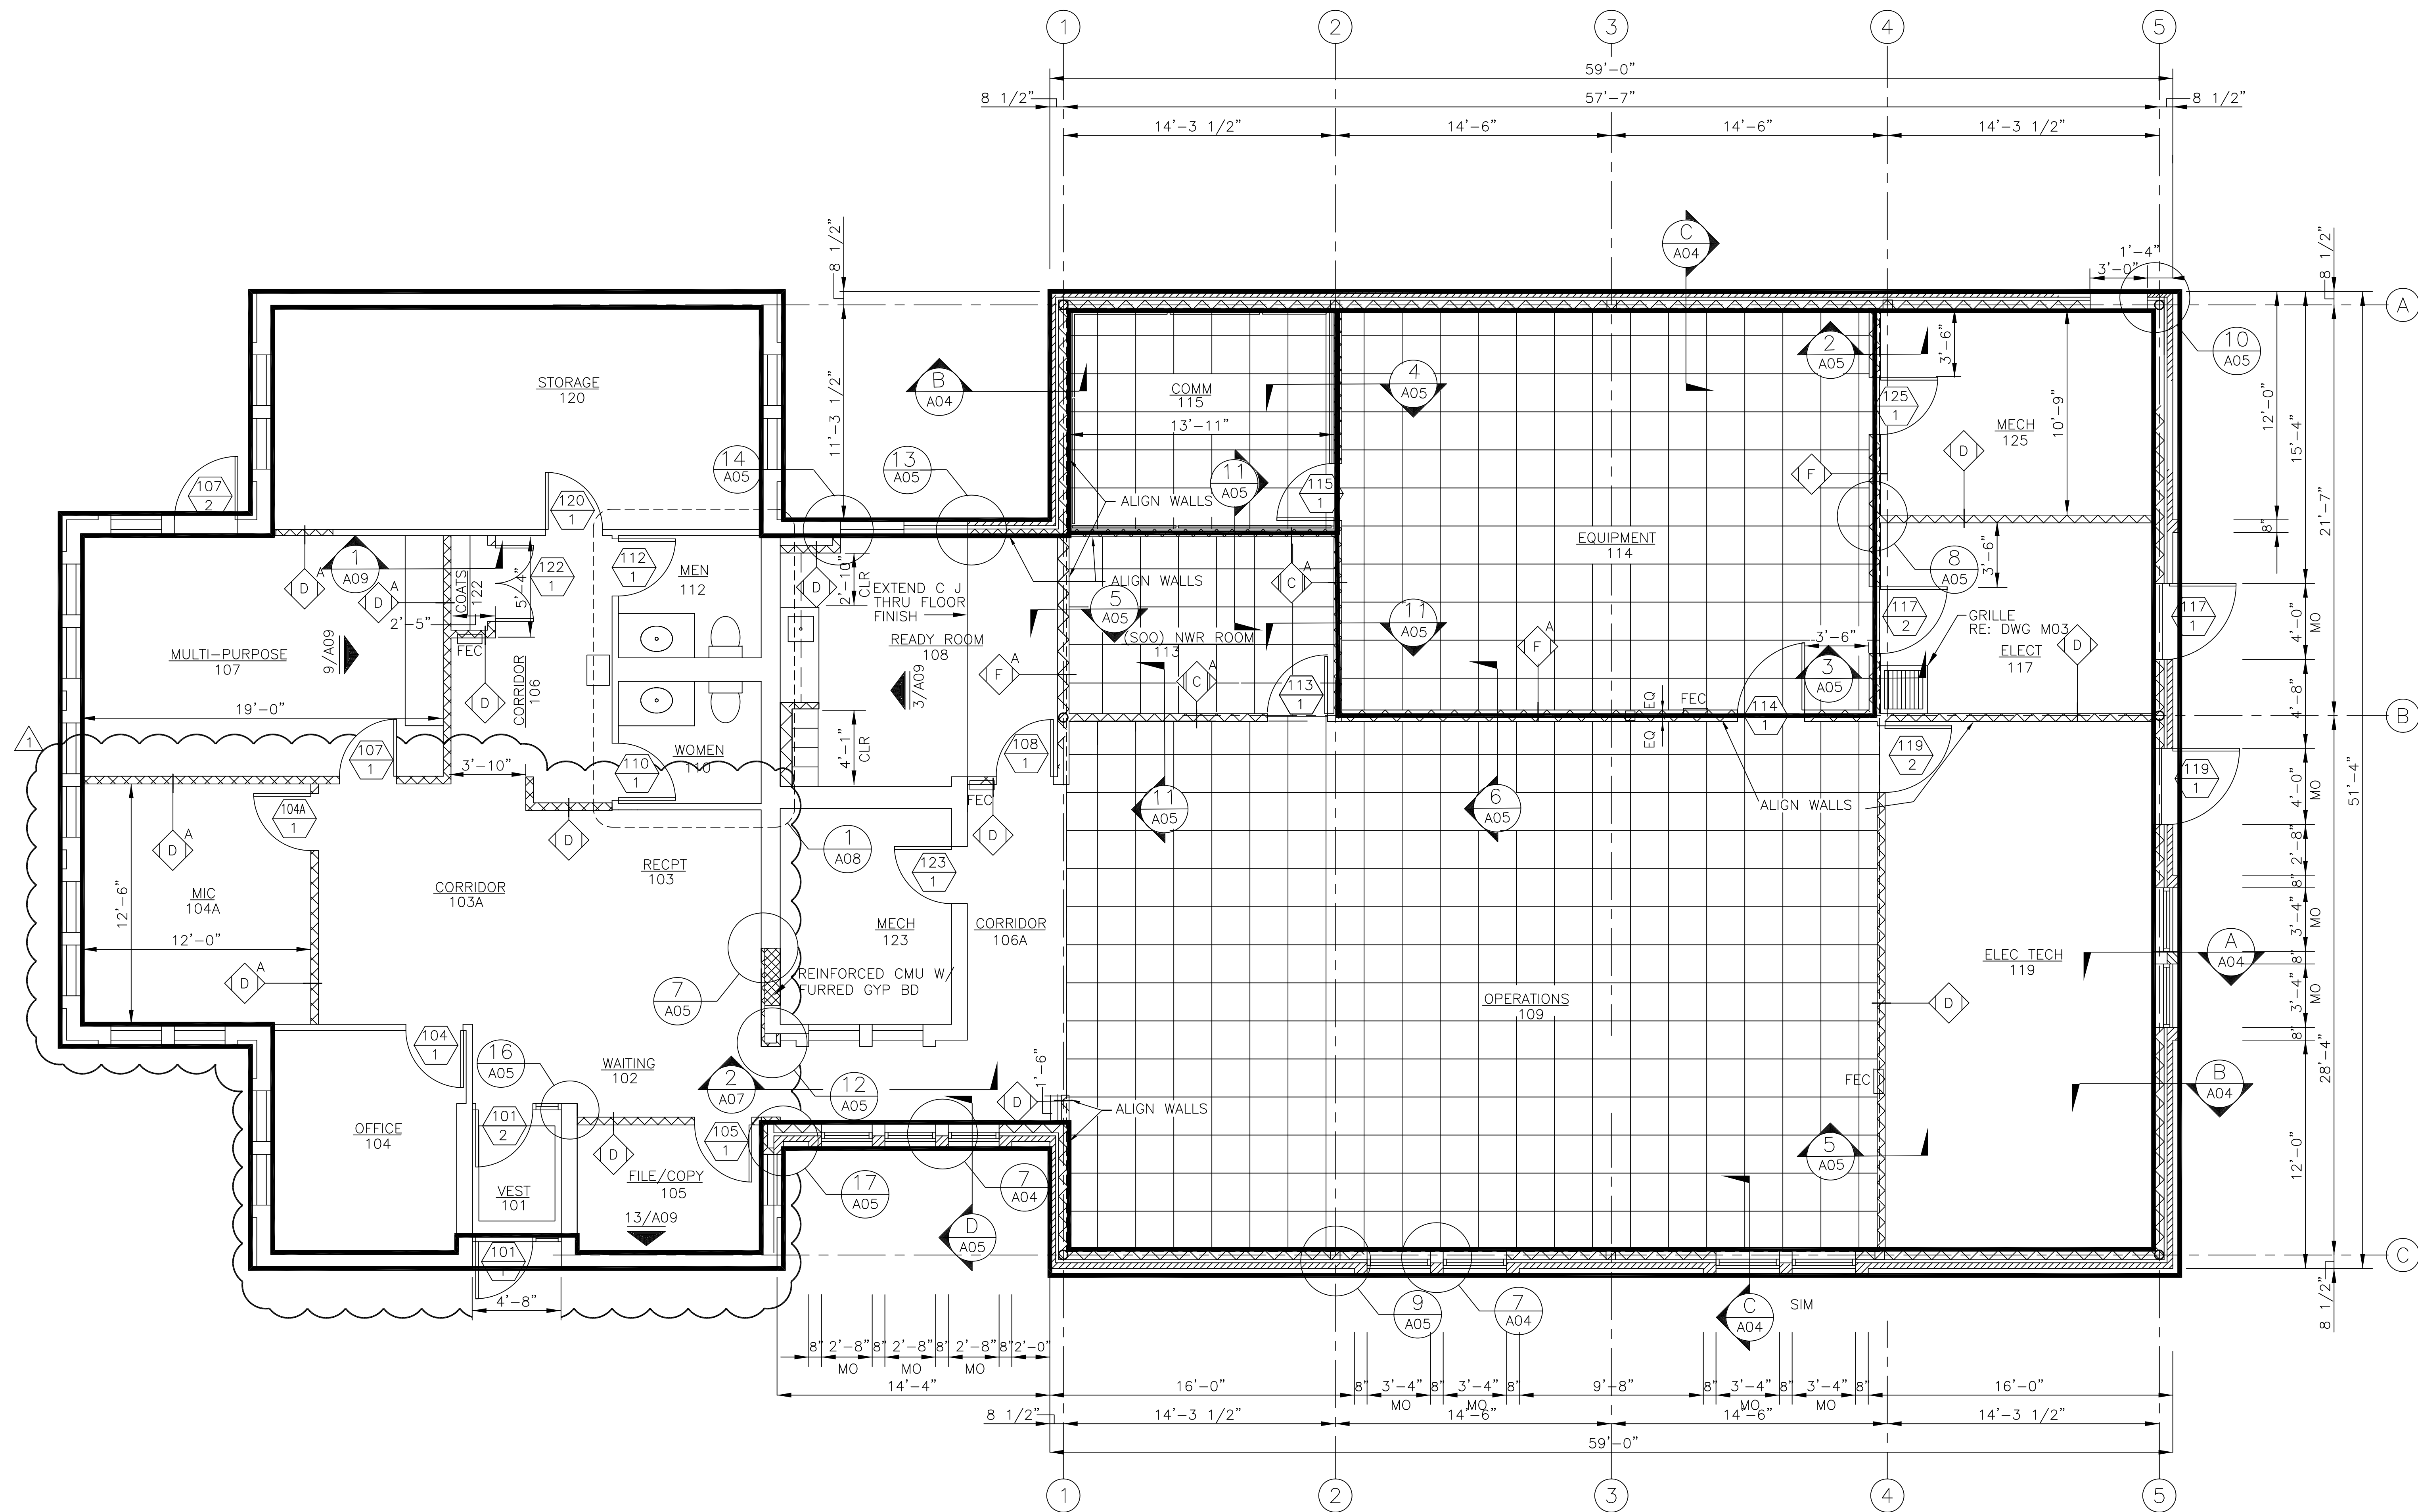


GENERAL NOTES

- FOR DRAWING LIST, ABBREVIATIONS AND PARTITION TYPES REFER TO DRAWING 101.
- DIMENSIONS ARE FROM COLUMN LINE TO FINISHED FACE OR FROM FINISHED FACE TO FINISHED FACE OF PARTITIONS UNLESS NOTED OTHERWISE.
- FINISH FLOOR ELEVATION = 0'-0" (EXCEPT AT ACCESS FLOOR) SEE DRAWING C05 FOR ACTUAL ELEVATIONS.
- SEE DRAWING C05 FOR SIDEWALK LOCATIONS.
- DO NOT SCALE DRAWINGS.
- PROVIDE VENETIAN BLINDS AT ALL NEW AND EXISTING EXTERIOR GLAZED OPENINGS EXCEPT AT VEST 101. BLIND WIDTH SHALL FIT INSIDE MULLIONS AT ALL LOCATIONS.
- PROVIDE A CONTINUOUS VAPOR RETARDER AT ALL NEW EXTERIOR WALLS, AND SEAL AT ALL EDGES AND PENETRATIONS.
- PROVIDE 3/4" PLYWOOD SHEETS MOUNTED WALL TO WALL (TYP FOR ALL WALLS IN COMM ROOM #115). PLYWOOD SHALL EXTEND FROM 2" BELOW ACCESS FLOOR TO CEILING ABOVE.
- FOR TYPICAL EXTERIOR WALL CONSTRUCTION AND NOTES SEE DETAIL ON SHEET A05.
- REFER TO ELEVATIONS, SHEET A03 FOR CONTROL AND RAKE JOINT LOCATIONS.
- REFER TO SHEET A11 FOR DDG/STORAGE BUILDING DRAWINGS.
- RENAMED MIC RM 104 TO OFFICE AND ADDED MIC RM 104A. RECPT RM 103. REMOVED BUILT-IN WORK STATION & WINDOW INTO VEST RM 101. FILE/COPY RM 105 SWITCH LOCATION WITH RECPT RM 103. RELABEL & RENUMBERED TRAINING 109A TO CORRIDOR 103A.

FLOOR PLAN
SCALE: 1/4"=1'-0"

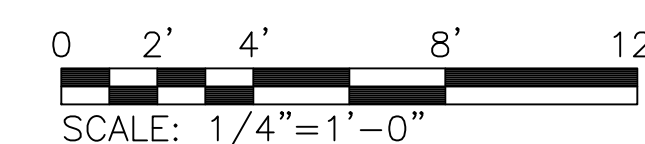

1. 05/13/96 S. BECKA						SEE NOTE 12					
NO.	DATE	PREPARED BY	CHECKED BY	FDI APPROVED	ACTR/COTR APPROVED	DESCRIPTION OF REVISION					
WFO / NEXRAD PROGRAM PROJECT NO. KA01						SPECIAL ENGINEERING PROGRAM OFFICE (SEPO)					
 FLUOR DANIEL GOULD EVANS ARCHITECTS, P.A. KANSAS CITY, MO. U.S.A.						DRAWN: D.S. HELTON CHECKED: SUPV. ENGR. ENGR./PROJ. MGR. ACTR./COTR.					
						SAFETY SHOULD ALWAYS BE FIRST WITH EVERY TASK YOU DO					
						 SPECIAL ENGINEERING PROGRAM OFFICE WEATHER FORECAST OFFICE JACKSON, KENTUCKY FLOOR PLAN					
						044131-	5	A02	KA	1	

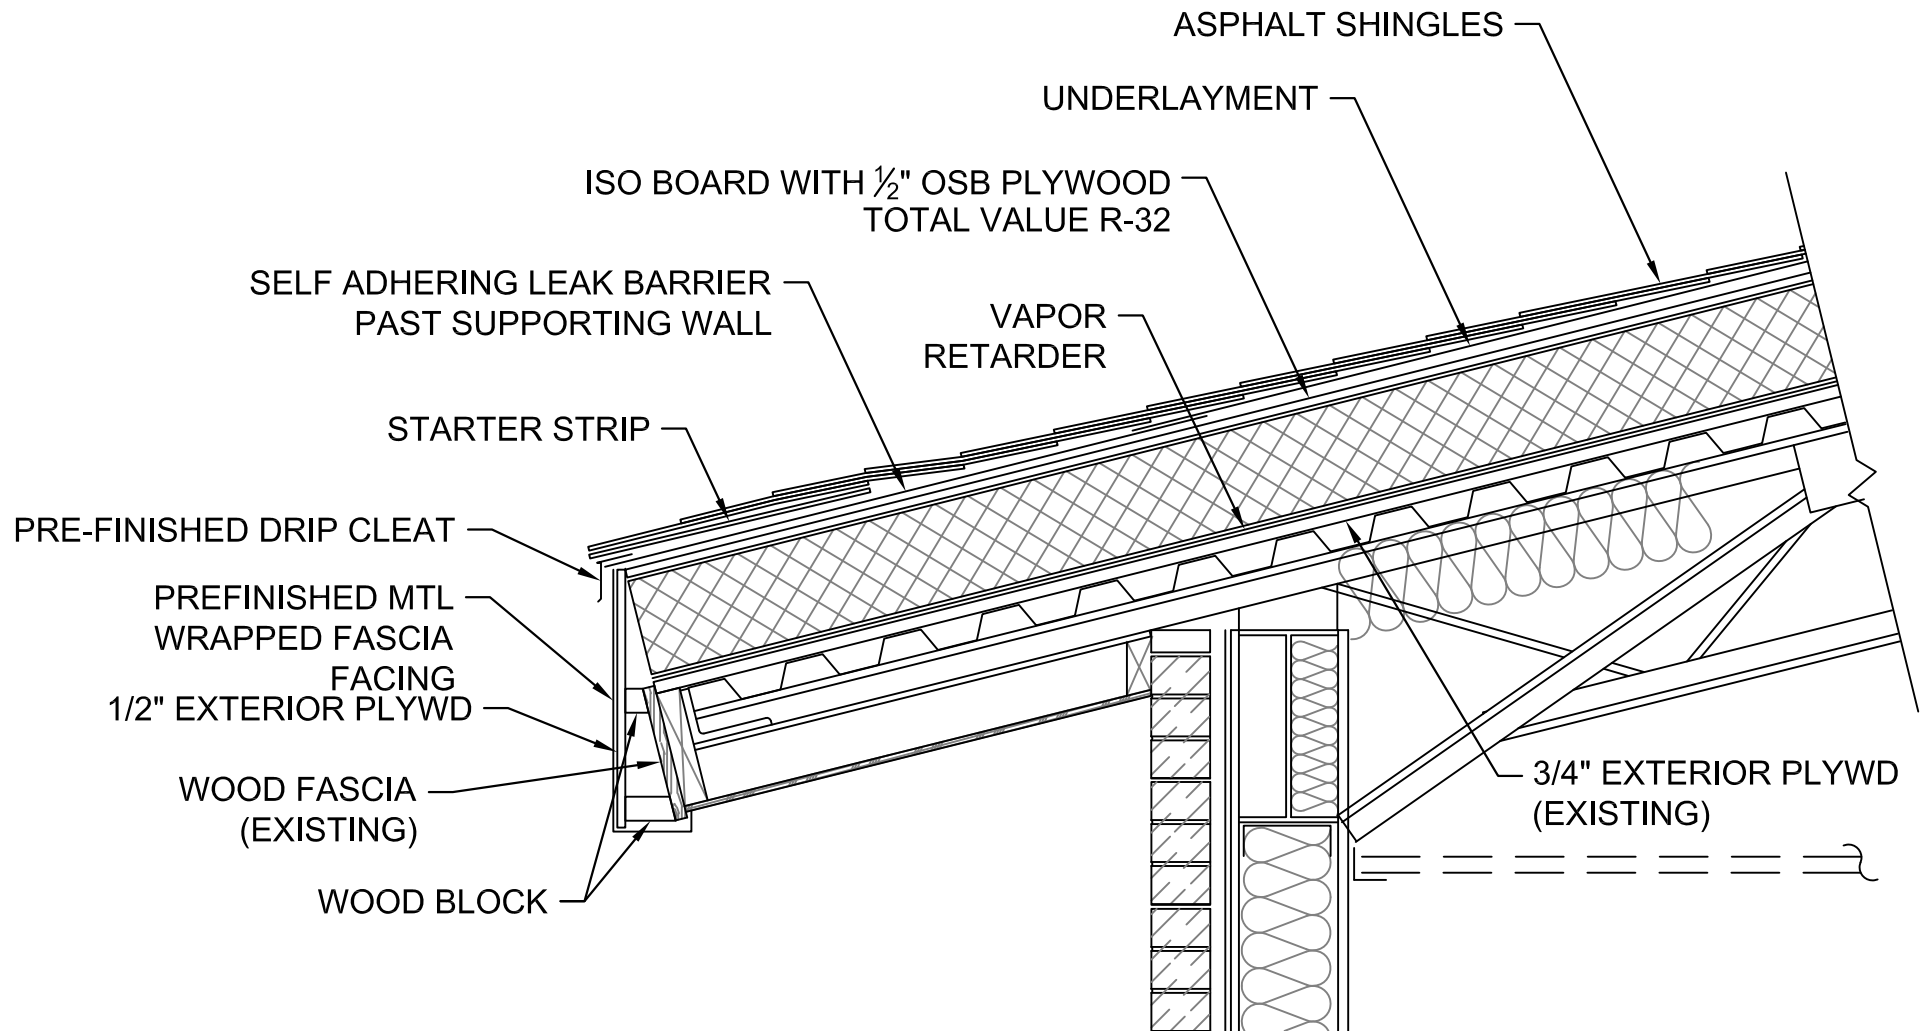

DRAWING BY:
STEVE BECKA


CHECKED/APPROVED BY:

DATE: MARCH 5, 2012

SCALE: 1" = 1'-0"

SHEET: _____ of _____

DRAWING NUMBER:
JKL-ROOF DETAIL

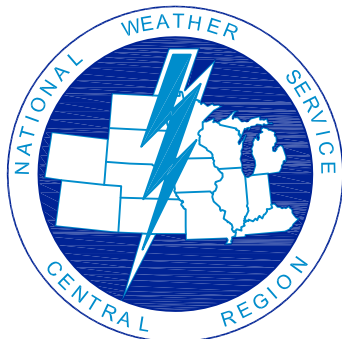

JACKSON, KENTUCKY

ROOF DETAIL

CENTRAL REGION HEADQUARTERS

REVISION

A blank sheet of white paper with horizontal blue ruling lines. The paper has rounded corners at the bottom and a vertical margin line on the left side. There are ten horizontal lines across the page.

REVISION