




Building 25007

1. Building Maps

- Sheet 1: Lead Sample Location Floor Plan
- Sheet 2: Asbestos Sample Location Floor Plan

2. Niton X-Ray Fluorescence (XRF) Analyzer Readings

3. Asbestos Containing Material (ACM) Laboratory Analysis

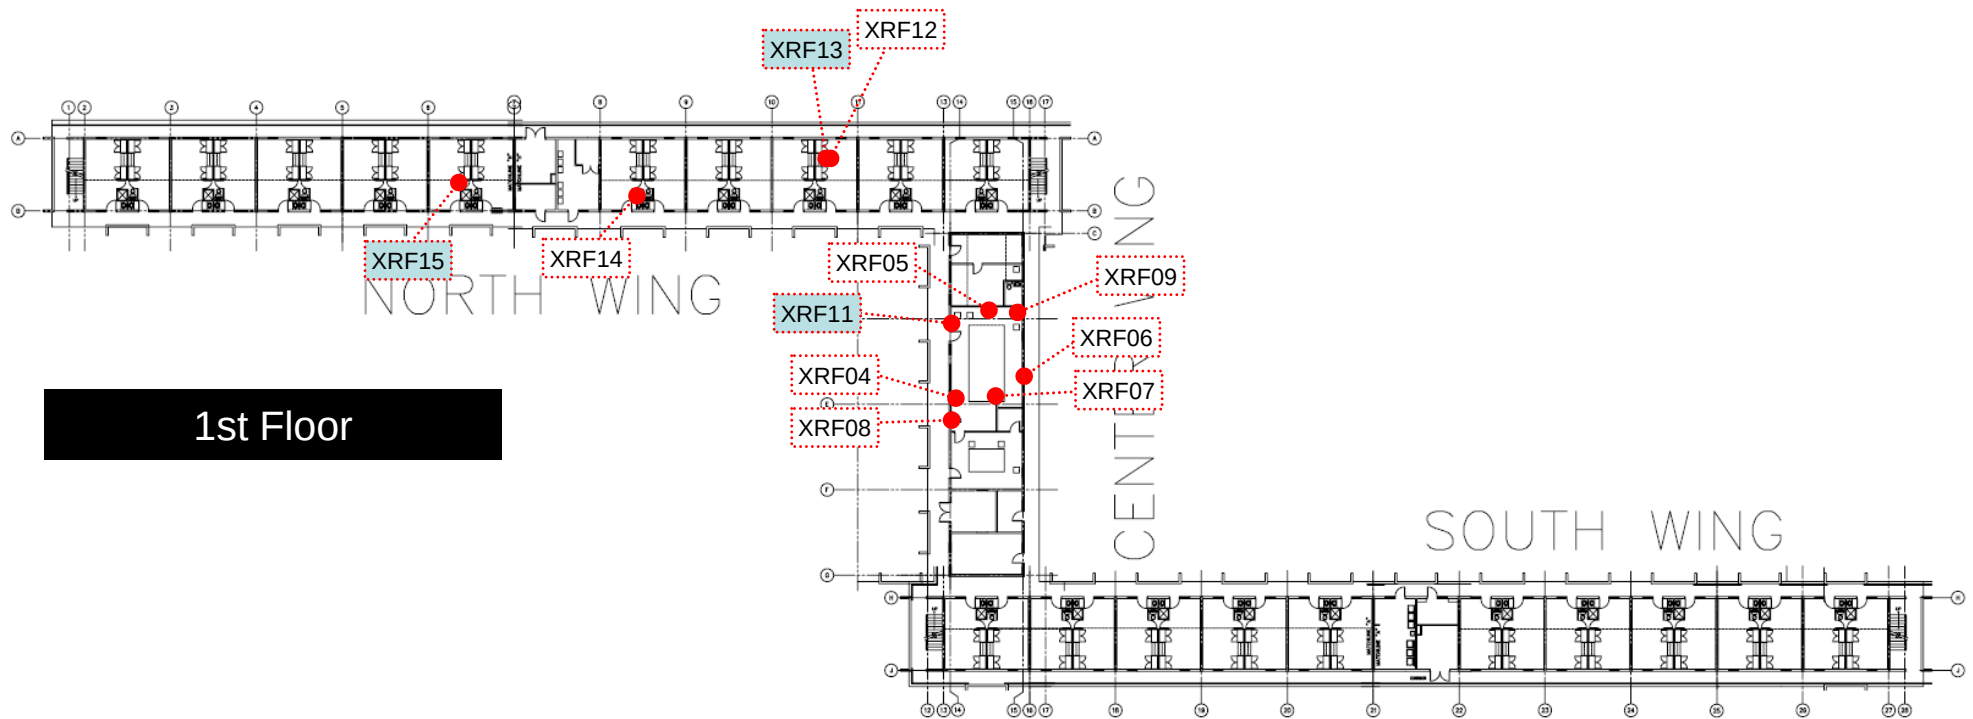

LEGEND

XRF Test Location	XRF00	Paint Chip Sample Location	LB00	Lead-Containing Paint (LCP)	XRF00	Lead-Base Paint (LBP)	XRF00
-------------------	-------	----------------------------	------	-----------------------------	-------	-----------------------	-------

Floor Plan Not to Scale



allied pacific environmental consulting


288 West O'Brien Drive Hagatna, Guam 96932
Tel/Fax: 671-477-7310 Fax: 671-477-7310

SHEET TITLE: Lead Sample Location Floor Plan

SHEET: 1

PROJECT: Inspections and Sampling for Buildings/Facilities at NSAAG

LOCATION: Building 25007, Andersen AFB, Guam

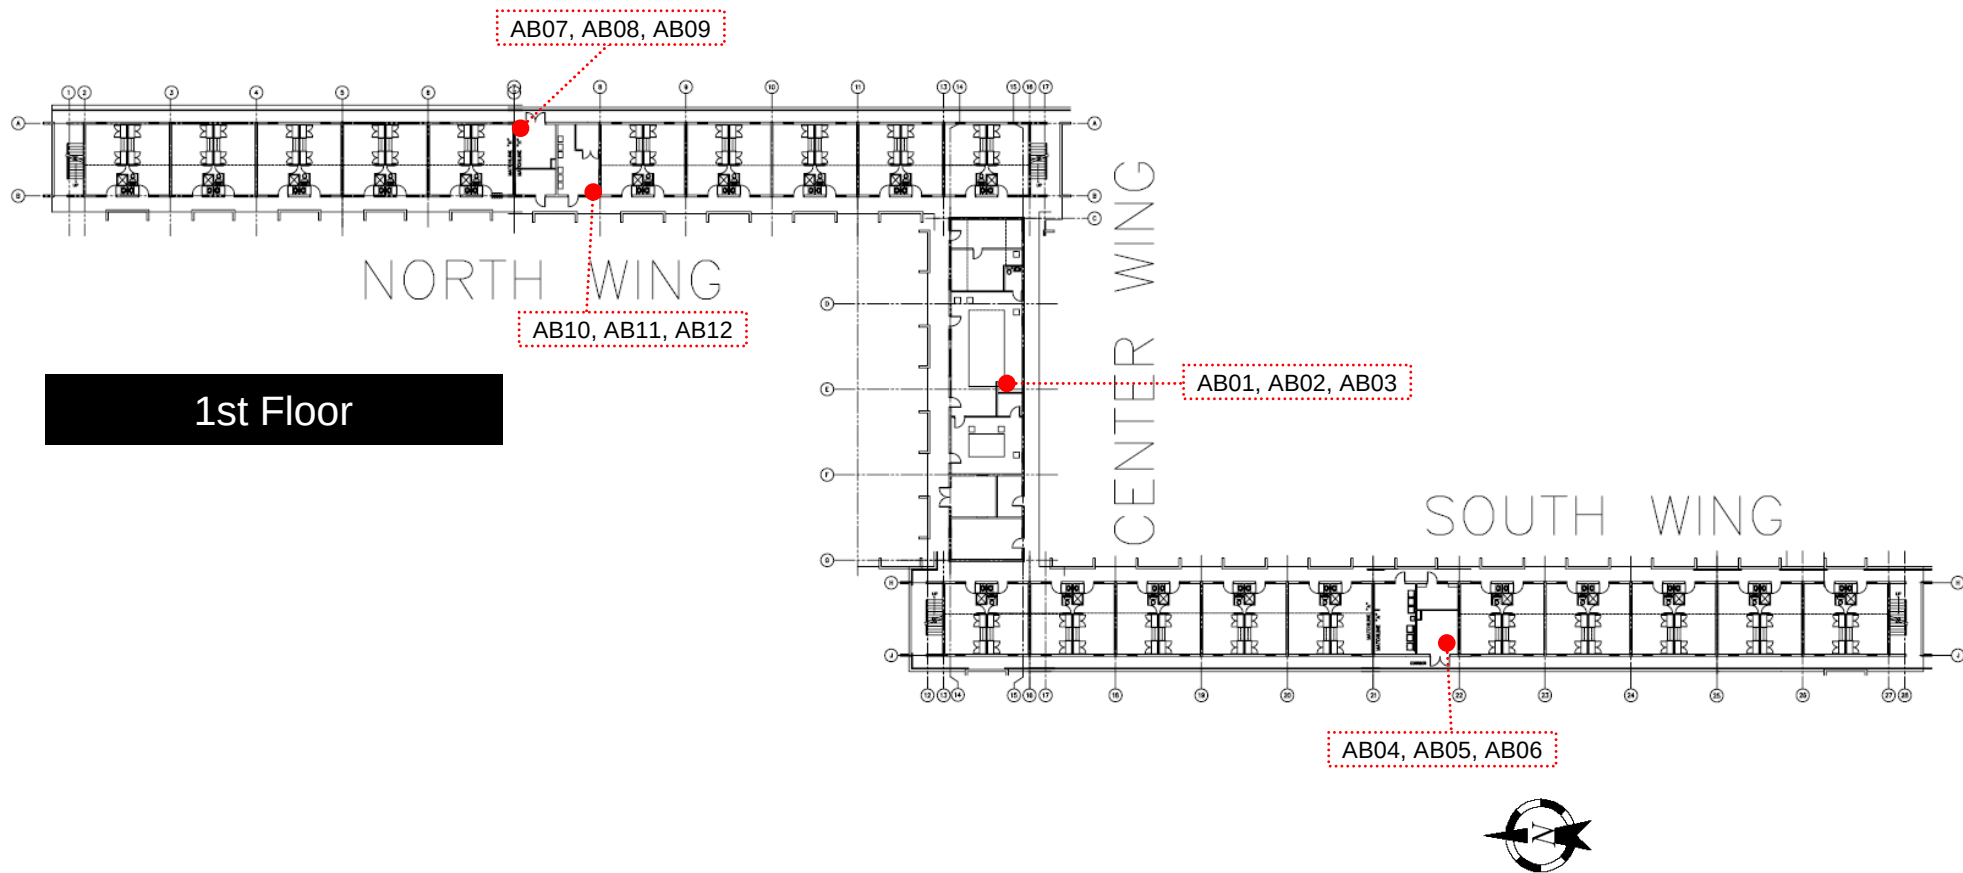

Floor Plan Not to Scale



allied pacific environmental consulting

288 West O'Brien Drive Hagatna, Guam 96932
Tel/Fax: 671-477-7310 Fax: 671-477-7310

SHEET TITLE: Asbestos Sample Location Floor Plan

SHEET: 2

PROJECT: Inspections and Sampling for Buildings/Facilities at NSAAG

LOCATION: Building 25007, Andersen AFB, Guam



allied pacific environmental consulting

Project Name: Asbestos and Lead-Based Paint Survey of Buildings/Facilities in Andersen AFB
Client: EMPSCO-Engineering, Inc.
Sample Date: April 18, 2013

Site: Building 25007, AAFB Guam

XRF #	Component	Substrate	Condition	Color	Sample Location	Results	Action Level	PbC	LBP	LCP
25007-CTP-XRF 1						Positive	1	1.2		
25007-CTP-XRF 2						Positive	1	1.1		
25007-CTP-XRF 3						Positive	1	1.1		
25007-CTP-XRF 4	Wall	Drywall	Intact	White	Game Room	Negative	1	0	No	No
25007-CTP-XRF 5	Wall	Drywall	Intact	White	Game Room	Negative	1	0	No	No
25007-CTP-XRF 6	Wall	Drywall	Intact	White	Game Room	Negative	1	0	No	No
25007-CTP-XRF 7	Wall	Drywall	Intact	White	Game Room	Negative	1	0	No	No
25007-CTP-XRF 8	Door	Metal	Intact	Brown	Game Room	Negative	1	0	No	No
25007-CTP-XRF 9	Door	Wood	Intact	Brown	Game Room Bathroom	Negative	1	0	No	No
25007-CTP-XRF 10						Null			No	No
25007-CTP-XRF 11	Wall	Concrete	Intact	White	Game Room	Negative	1	0.12	No	Yes
25007-CTP-XRF 12	Door	Wood	Intact	White	Room 118	Negative	1	0	No	No
25007-CTP-XRF 13	Wall	Ceramic Tile	Intact	Beige	Room 118	Negative	1	0.01	No	Yes
25007-CTP-XRF 14	Wall	Ceramic Tile	Intact	Maroon	Room 113 Bathroom	Negative	1	0	No	No
25007-CTP-XRF 15	Wall	Ceramic Tile	Intact	Green	Room 109 Bathroom	Negative	1	0.28	No	Yes
25007-CTP-XRF 16						Positive	1	1.1		
25007-CTP-XRF 17						Positive	1	1.1		
25007-CTP-XRF 18						Positive	1	1		

XRF: X-ray fluorescence **LBP:** Lead-base Paint **LCP:** Lead-containing Paint **PbC:** Lead Concentration

530-274-1470 or 1-800-MACS LAB

Allied Pacific Environmental Consul
288 West O'Brien Drive

Hagatna

GU 96910-5130

Analyst: _____

DD

(signature)

Person to contact: Andrew Apatang

Contact phone: 671-477-7310

emailed

Sampled by: Andrew Apatang

Sampled on: April 25, 2013

Analyzed on: June 14, 2013

at: 07:35

Reported on: 00/00/00

at: 00:00

Corresponding invoice number: 232788

Laboratory manager: _____

(signature)

Job Description: Buiding 25007 Andersen Air Force Base, Guam

Lab Sample Number	Client Sample Number and Description	Asbestos detected?	Fibers present	Remarks
L232788-1	25007-AA-AB01 24x24 White Smooth Ceiling Tile observed throughout Facility	No	95% Cellulose	Off-white ceiling tile. Balance of sample is unspecified non-fibrous material.
L232788-2	25007-AA-AB02 24x24 White Smooth Ceiling Tile observed throughout Facility	No	95% Cellulose	Off-white ceiling tile. Balance of sample is unspecified non-fibrous material.
L232788-3	25007-AA-AB03 24x24 White Smooth Ceiling Tile observed throughout Facility	No	95% Cellulose	Off-white ceiling tile. Balance of sample is unspecified non-fibrous material.
L232788-4	25007-AA-AB04 White Tile Grout associated with 12x12 Beige Ceramic Tile observed throughout Facility	No	< 1% Cellulose	Off-white grout. Balance of sample is unspecified non-fibrous material and cementitious.
L232788-5	25007-AA-AB05 White Tile Grout associated with 12x12 Beige Ceramic Tile observed throughout Facility	No	< 1% Cellulose	Off-white grout. Balance of sample is unspecified non-fibrous material and cementitious.

* Chrysotile, Amosite, Crocidolite, Tremolite, Actinolite, and Anthophyllite are asbestos fibers. PC =Point Counted



This report shall not be reproduced except in full without written approval of MACS Lab, Inc. This report relates only to the items tested. Samples will be destroyed after one month. Test per 40 Code of Federal Reg. Chap I (1-1-87) Part 763, Subpart F, Appendix A or current EPA method. Percentages are approximate. MACS Lab is an accredited laboratory of the National Voluntary Laboratory Accreditation Program (NVLAP) and is Lab Code 101948-0. No product endorsement by NVLAP or any agency of the U.S. Government may be claimed as a result of this analysis. Calif Dept of Health ELAP #2027. This method is not reliable for analysis of tile or other materials when fiber size is less than 10µ. TEM analysis should be used. Method Detection limit for asbestos is 1% per CA law. See QC page attached to this page for blank and retest data.

530-274-1470 or 1-800-MACS LAB

Lab Sample Number	Client Sample Number and Description	Asbestos detected?	Fibers present	Remarks
L232788-6	25007-AA-AB06 White Tile Grout associated with 12x12 Beige Ceramic Tile observed throughout Facility	No	< 1% Cellulose	Off-white grout. Balance of sample is unspecified non-fibrous material and cementitious.
L232788-7	25007-AA-AB07 Black Covebase over Gray Glue observed throughout Facility	No	< 1% Cellulose	Black covebase. Balance of sample is unspecified non-fibrous material.
L232788-8	25007-AA-AB07a Glue on Covebase	No	1% Cellulose	Yellow adhesive. Balance of sample is unspecified non-fibrous material.
Layer				
L232788-9	25007-AA-AB08 Black Covebase over Gray Glue observed throughout Facility	No	< 1% Cellulose	Black covebase. Balance of sample is unspecified non-fibrous material.
L232788-10	25007-AA-AB08a Glue on Covebase	No	< 1% Cellulose	Yellow adhesive. Balance of sample is unspecified non-fibrous material.
Layer				
L232788-11	25007-AA-AB09 Black Covebase over Gray Glue observed throughout Facility	No	No Fibers	Black covebase. Balance of sample is unspecified non-fibrous material.
L232788-12	25007-AA-AB09a Glue on Covebase	No	< 1% Cellulose	Yellow adhesive. Balance of sample is unspecified non-fibrous material.
Layer				
L232788-13	25007-AA-AB10 Drywall - Gypsum Wallboard observed throughout Facility	No	2% Cellulose	Off-white gypsum wallboard. Balance of sample is unspecified non-fibrous material.
L232788-14	25007-AA-AB11 Drywall - Gypsum Wallboard observed throughout Facility	No	3% Cellulose	Off-white gypsum wallboard. Balance of sample is unspecified non-fibrous material.

* Chrysotile, Amosite, Crocidolite, Tremolite, Actinolite, and Anthophyllite are asbestos fibers. PC =Point Counted



This report shall not be reproduced except in full without written approval of MACS Lab, Inc. This report relates only to the items tested. Samples will be destroyed after one month. Test per 40 Code of Federal Reg. Chap I (1-1-87) Part 763, Subpart F, Appendix A or current EPA method. Percentages are approximate. MACS Lab is an accredited laboratory of the National Voluntary Laboratory Accreditation Program (NVLAP) and is Lab Code 101948-0. No product endorsement by NVLAP or any agency of the U.S. Government may be claimed as a result of this analysis. Calif Dept of Health ELAP #2027. This method is not reliable for analysis of tile or other materials when fiber size is less than 10µ. TEM analysis should be used. Method Detection limit for asbestos is 1% per CA law. See QC page attached to this page for blank and retest data .

530-274-1470 or 1-800-MACS LAB

Lab Sample Number	Client Sample Number and Description	Asbestos detected?	Fibers present	Remarks
L232788-15	25007-AA-AB12 Drywall - Gypsum Wallboard observed throughout Facility	No	>1%to2% Cellulose	Off-white gypsum wallboard. Balance of sample is unspecified non-fibrous material.

* Chrysotile, Amosite, Crocidolite, Tremolite, Actinolite, and Anthophyllite are asbestos fibers. PC =Point Counted



This report shall not be reproduced except in full without written approval of MACS Lab, Inc. This report relates only to the items tested. Samples will be destroyed after one month. Test per 40 Code of Federal Reg. Chap I (1-1-87) Part 763, Subpart F, Appendix A or current EPA method. Percentages are approximate. MACS Lab is an accredited laboratory of the National Voluntary Laboratory Accreditation Program (NVLAP) and is Lab Code 101948-0. No product endorsement by NVLAP or any agency of the U.S. Government may be claimed as a result of this analysis. Calif Dept of Health ELAP #2027. This method is not reliable for analysis of tile or other materials when fiber size is less than 10 μ . TEM analysis should be used. Method Detection limit for asbestos is 1% per CA law. See QC page attached to this page for blank and retest data .

MACS Lab, Inc.431 Crown Point Cir Ste 120
Grass Valley, CA 95945-9531

530-274-1470 or 1-800-MACS LAB

Bulk Asbestos Analysis**Method: EPA-600/M4-82-020****QA Report**Allied Pacific Environmental Consul
288 West O'Brien Drive

Hagatna

GU 96910-5130

Laboratory manager: _____

(signature)

Lab Sample Number	Client Sample Number and Description	Asbestos detected?	Fibers present	Remarks
L232788-2	25007-AA-AB02 24x24 White Smooth Ceiling Tile observed throughout Facility	No	93% Cellulose	Ceiling tile. Balance of sample is unspecified non-fibrous material.
L232788-3	25007-AA-AB03 24x24 White Smooth Ceiling Tile observed throughout Facility	No	93% Cellulose	Ceiling tile. Balance of sample is unspecified non-fibrous material.
L232788-4	25007-AA-AB04 White Tile Grout associated with 12x12 Beige Ceramic Tile observed throughout Facility	No	No Fibers	Grout. Balance of sample is cementitious and unspecified non-fibrous material.
L232788-13	25007-AA-AB10 Drywall - Gypsum Wallboard observed throughout Facility	No	3% Cellulose	Drywall balance of sample is unspecified non-fibrous material.

* Chrysotile, Amosite, Crocidolite, Tremolite, Actinolite, and Anthophyllite are asbestos fibers. N.D.=None Detected PC =Point Counted



This report shall not be reproduced except in full without written approval of MACS Lab, Inc. This report relates only to the items tested. Samples will be destroyed after one month. Test per 40 Code of Federal Reg. Chap I (1-1-87) Part 763, Subpart F, Appendix A or current EPA method. Percentages are approximate. MACS Lab is an accredited laboratory of the National Voluntary Laboratory Accreditation Program (NVLAP) and is Lab Code 101948-0. No product endorsement by NVLAP or any agency of the U.S. Government may be claimed as a result of this analysis. Calif Dept of Health ELAP #2027. This method is not reliable for analysis of tile or other materials when fiber size is less than 10µ. TEM analysis should be used. Method Detection limit for asbestos is 1% per CA law. See QC page attached to this page for blank and retest data.