
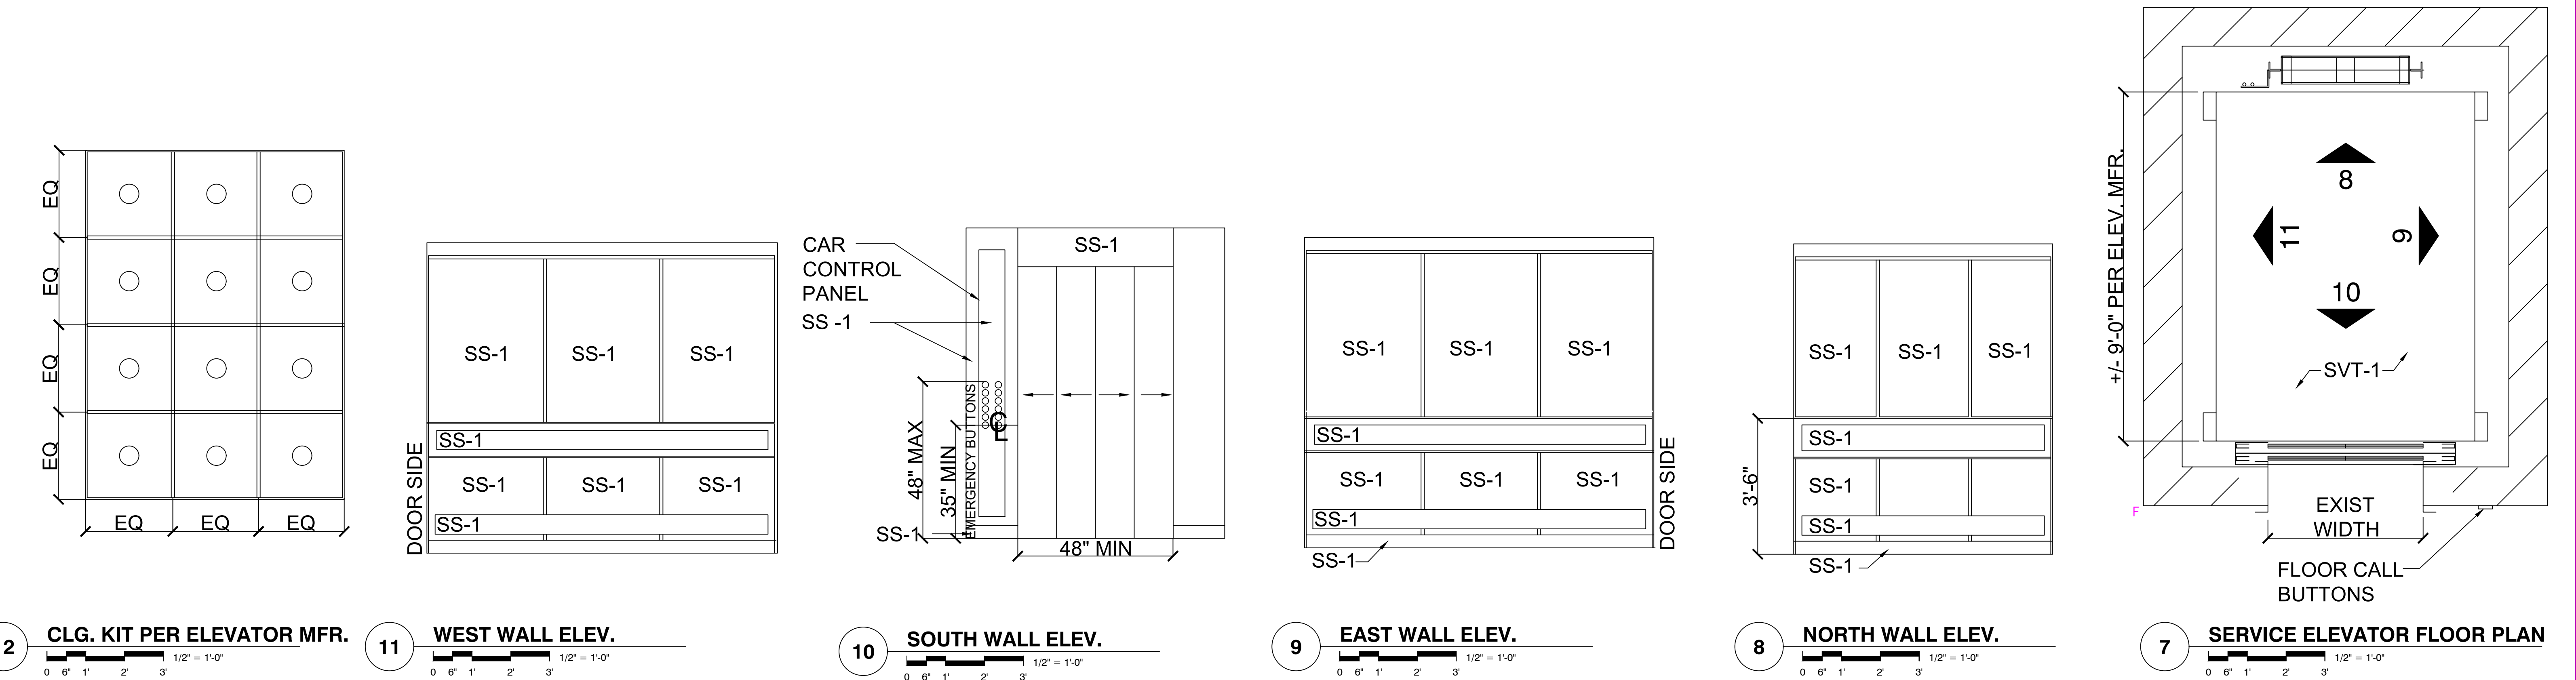


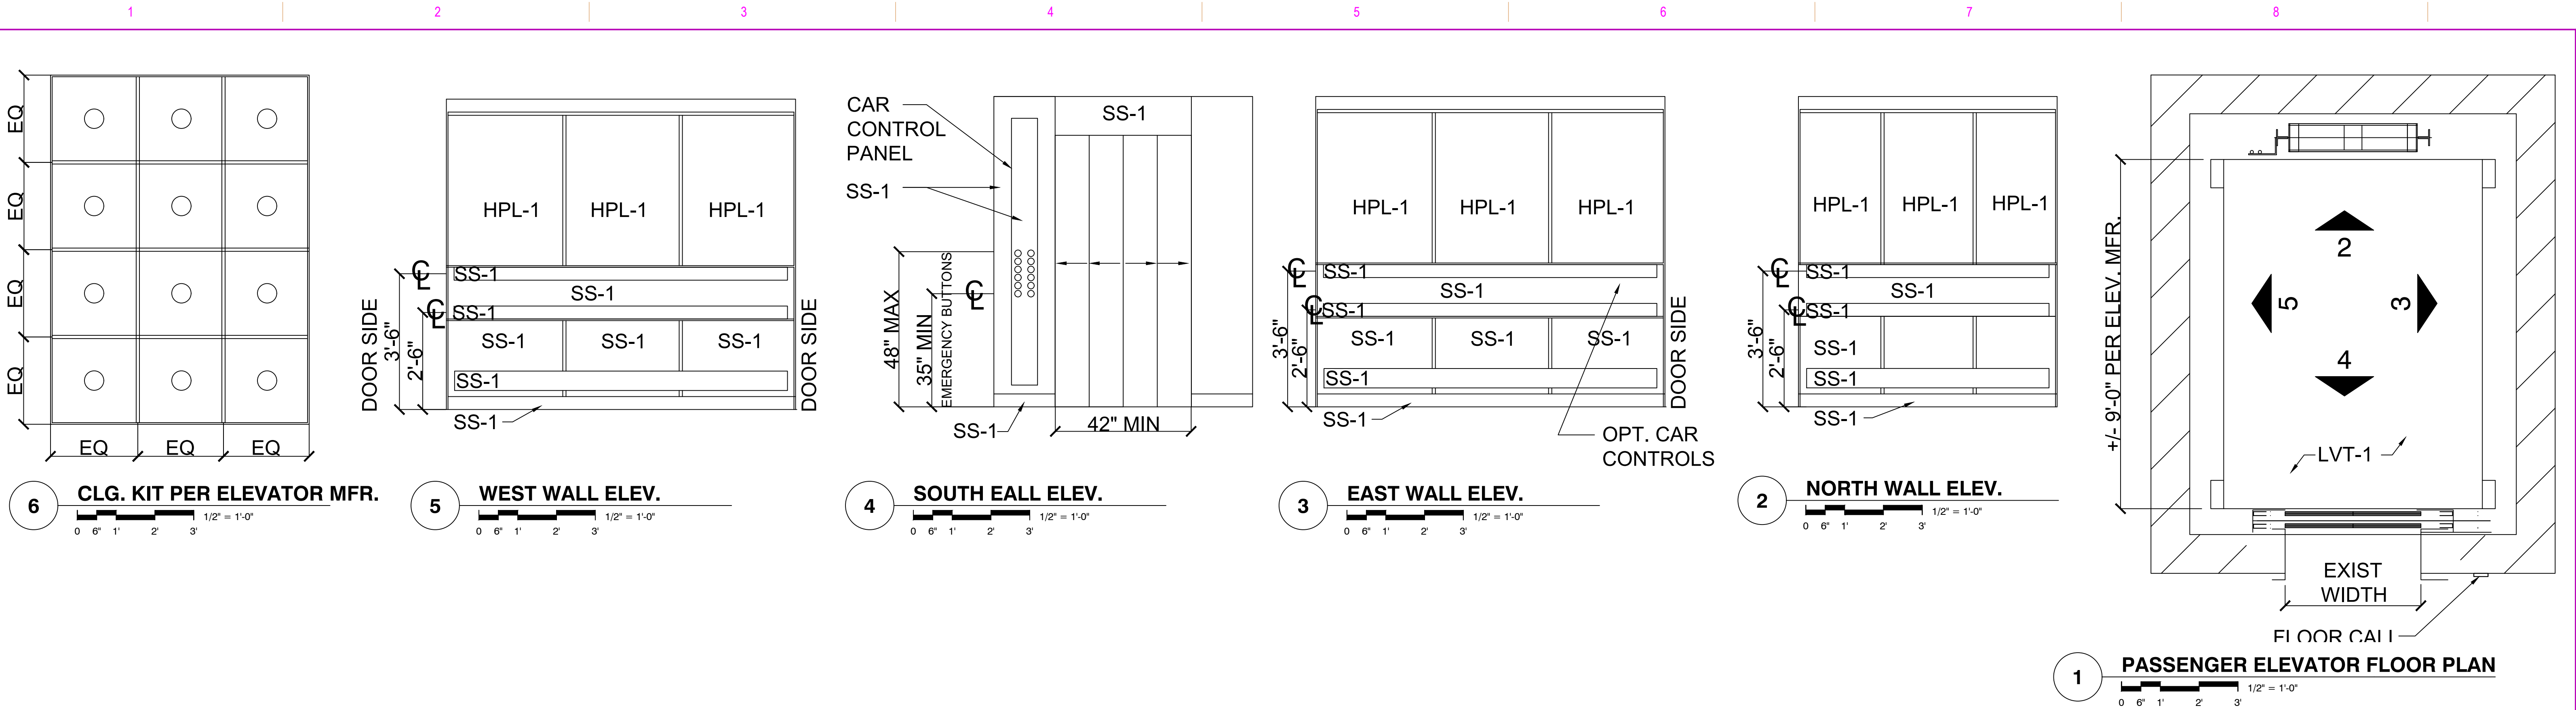

CONSULTANTS:		ARCHITECT/ENGINEERS:		STAMP:		Drawing Title Elevator Floor Plan, Elevations, and Ceiling Plan		Phase		Project Title Department of Veterans Affairs' Elevator Standards		Project Number	
						Approved: Project Director				Location Department of Veterans Affairs		Building Number	
Issued:		Date:		VEG 18.10						Issue Date 03.30.2026		Checked CE	
												Drawing Number	