


DEMO KEYNOTE LEGEND	
Type Mark	Keynote
01	REMOVE DIVIDING WALL
02	REMOVE DOOR
03	REMOVE CARPET TILE FLOORING
04	PODIUMS TO BE REMOVED AND RETURNED TO THE VA.
05	REMOVE DIVIDING WALL CLOSET
06	DEMO SMARTBOARD
07	LIMIT OF CARPET REPLACEMENT
12	EXISTING STRUCTURAL SUPPORT FOR EXISTING TRACK MAY NEED TO BE REMOVED AND REPLACED WITH NEW SUPPORTS.

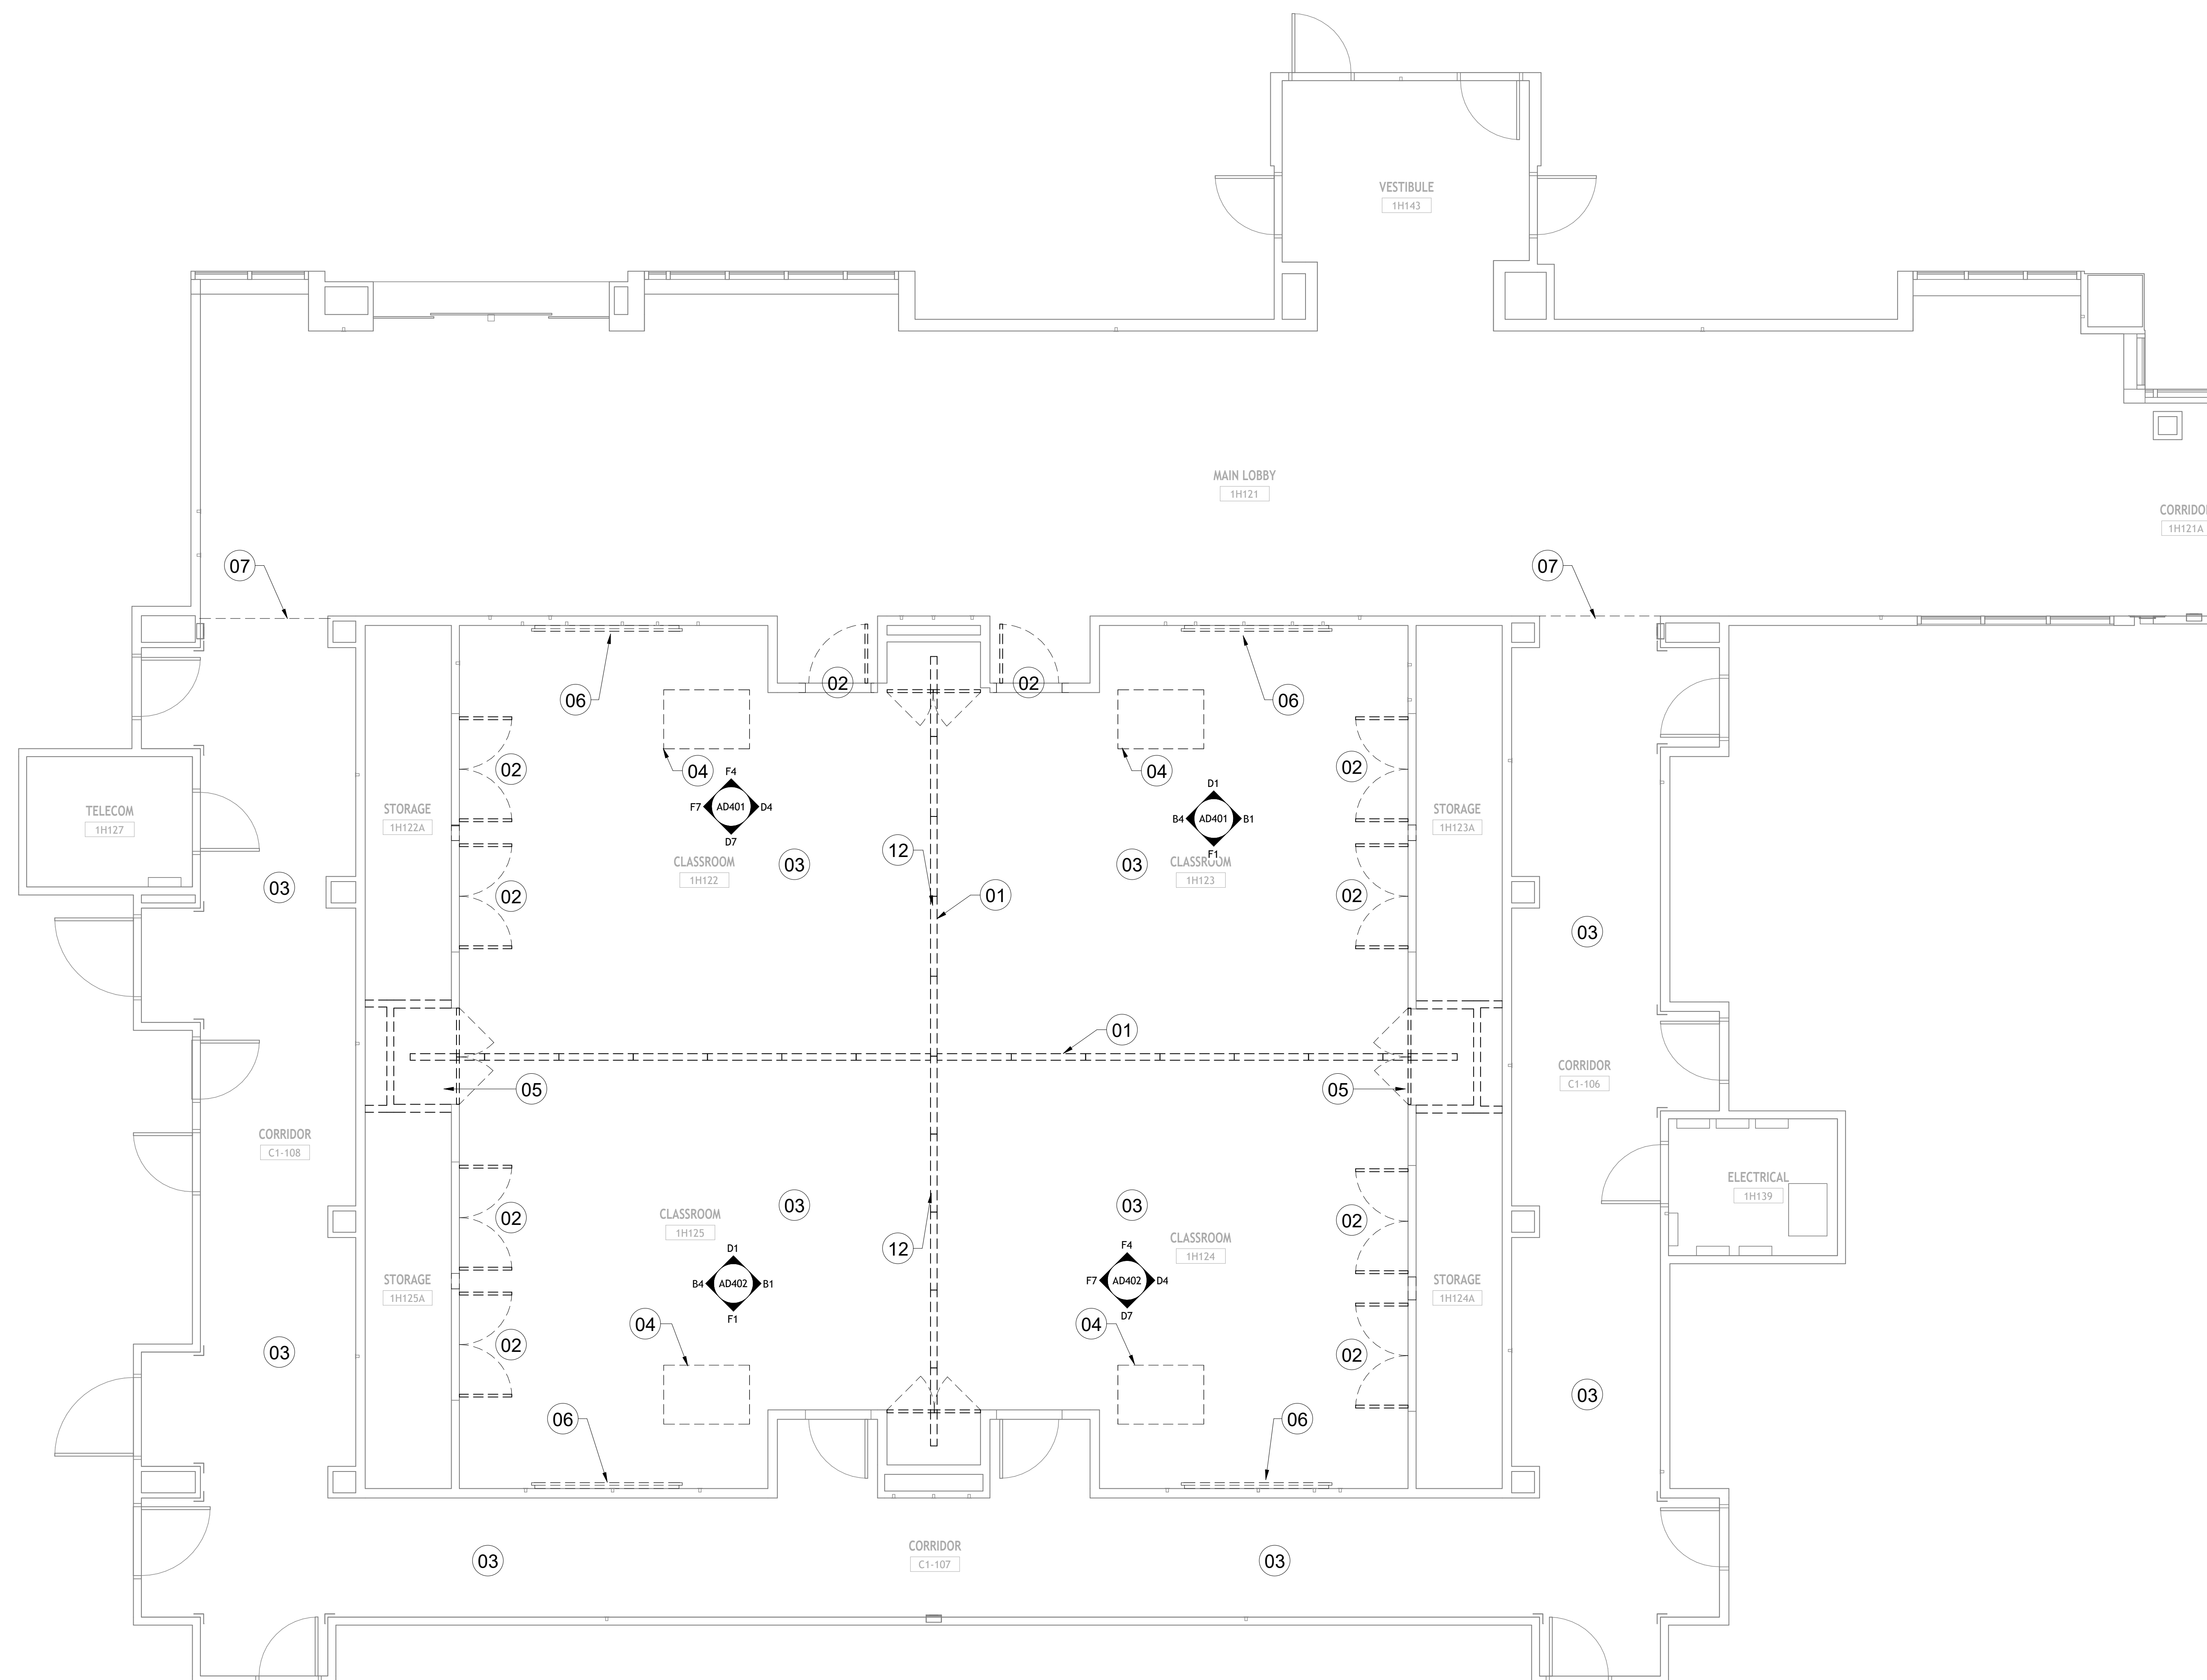


F1 DEMO WORK FLOOR PLAN
1/4" = 1'-0"

NOT FOR CONSTRUCTION

		CONSULTANT	ARCHITECT/ENGINEER OF RECORD	STAMP	VASNHCS Project Management and Construction Management Services  U.S. Department of Veterans Affairs	Drawing Title DEMO WORK FLOOR PLAN Approved: Project Manager/COR Department of Veteran Affairs, NCA POC: Phone: Email:	Phase DESIGN SUPPORT	Project Title ASSIGNMENT No. 49: DESIGN SUPPORT FOR RENOVATE EDUCATION BLDG TRAINING HUB Location Las Vegas, NV Issue Date 03/13/2026 Checked Checker Drawn Author	Project Number 593-26-302 Building Number 001 Drawing Number AD101
--	--	------------	------------------------------	-------	--	---	---	---	---


DEMO KEYNOTE LEGEND	
Type Mark	Keynote
01	REMOVE DIVIDING WALL
05	REMOVE DIVIDING WALL CLOSET
08	DEMO GYPSUM BOARD SOFFIT
09	REMOVE CEILING MOUNTED PROJECTOR.
10	REMOVE CEILING MOUNTED PROJECTOR SCREEN
12	EXISTING STRUCTURAL SUPPORT FOR EXISTING TRACK MAY NEED TO BE REMOVED AND REPLACED WITH NEW SUPPORTS.
13	DEMO CEILING TILES AND GRIDS.

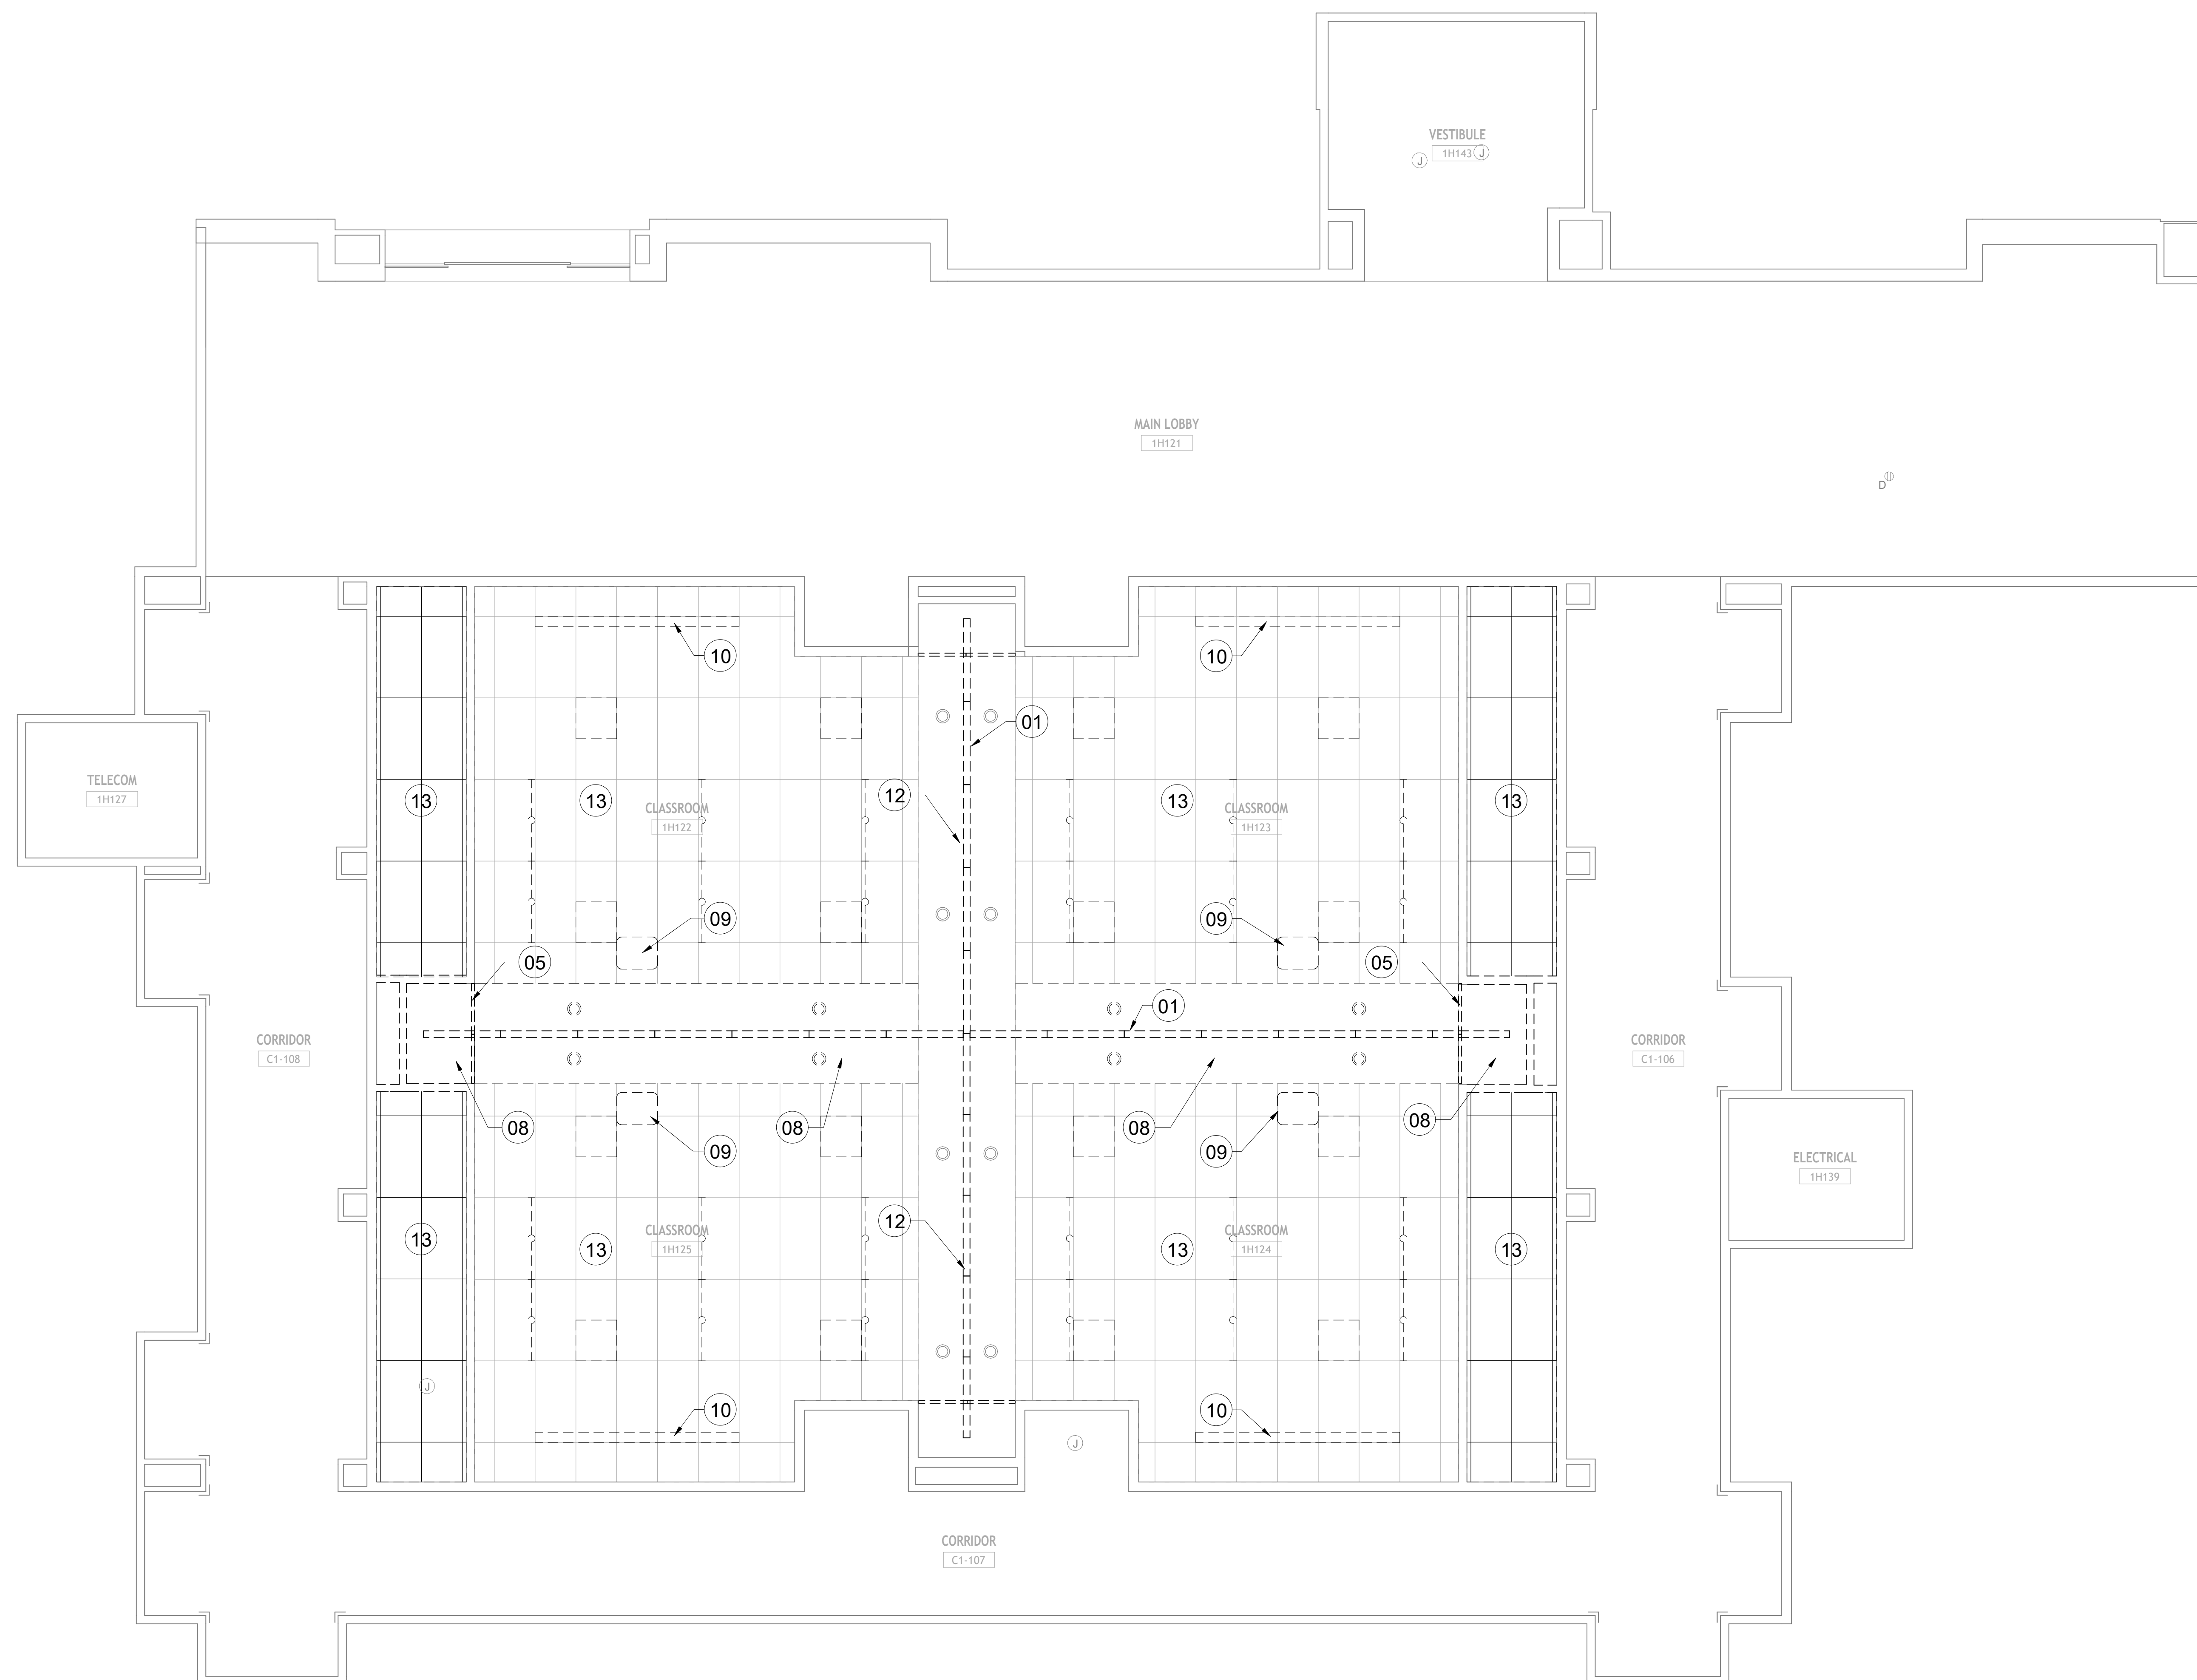

(F1) DEMO WORK REFLECTED CEILING PLAN
1/4" = 1'-0"



		CONSULTANT	ARCHITECT/ENGINEER OF RECORD	STAMP	VASNHCS	Drawing Title	Project Title	Project Title	Project Number
					Project Management and Construction Management Services	DEMO WORK REFLECTED CEILING PLAN	DESIGN SUPPORT	ASSIGNMENT No. 49: DESIGN SUPPORT FOR RENOVATE EDUCATION BLDG TRAINING HUB	593-26-302
						Approved: Project Manager/COR Department of Veteran Affairs, NCA		Location	Building Number
						POC:		Las Vegas, NV	001
						Phone:		Drawing Number	
						Email:			AD102
Revisions:	Date:	 U.S. Department of Veterans Affairs							

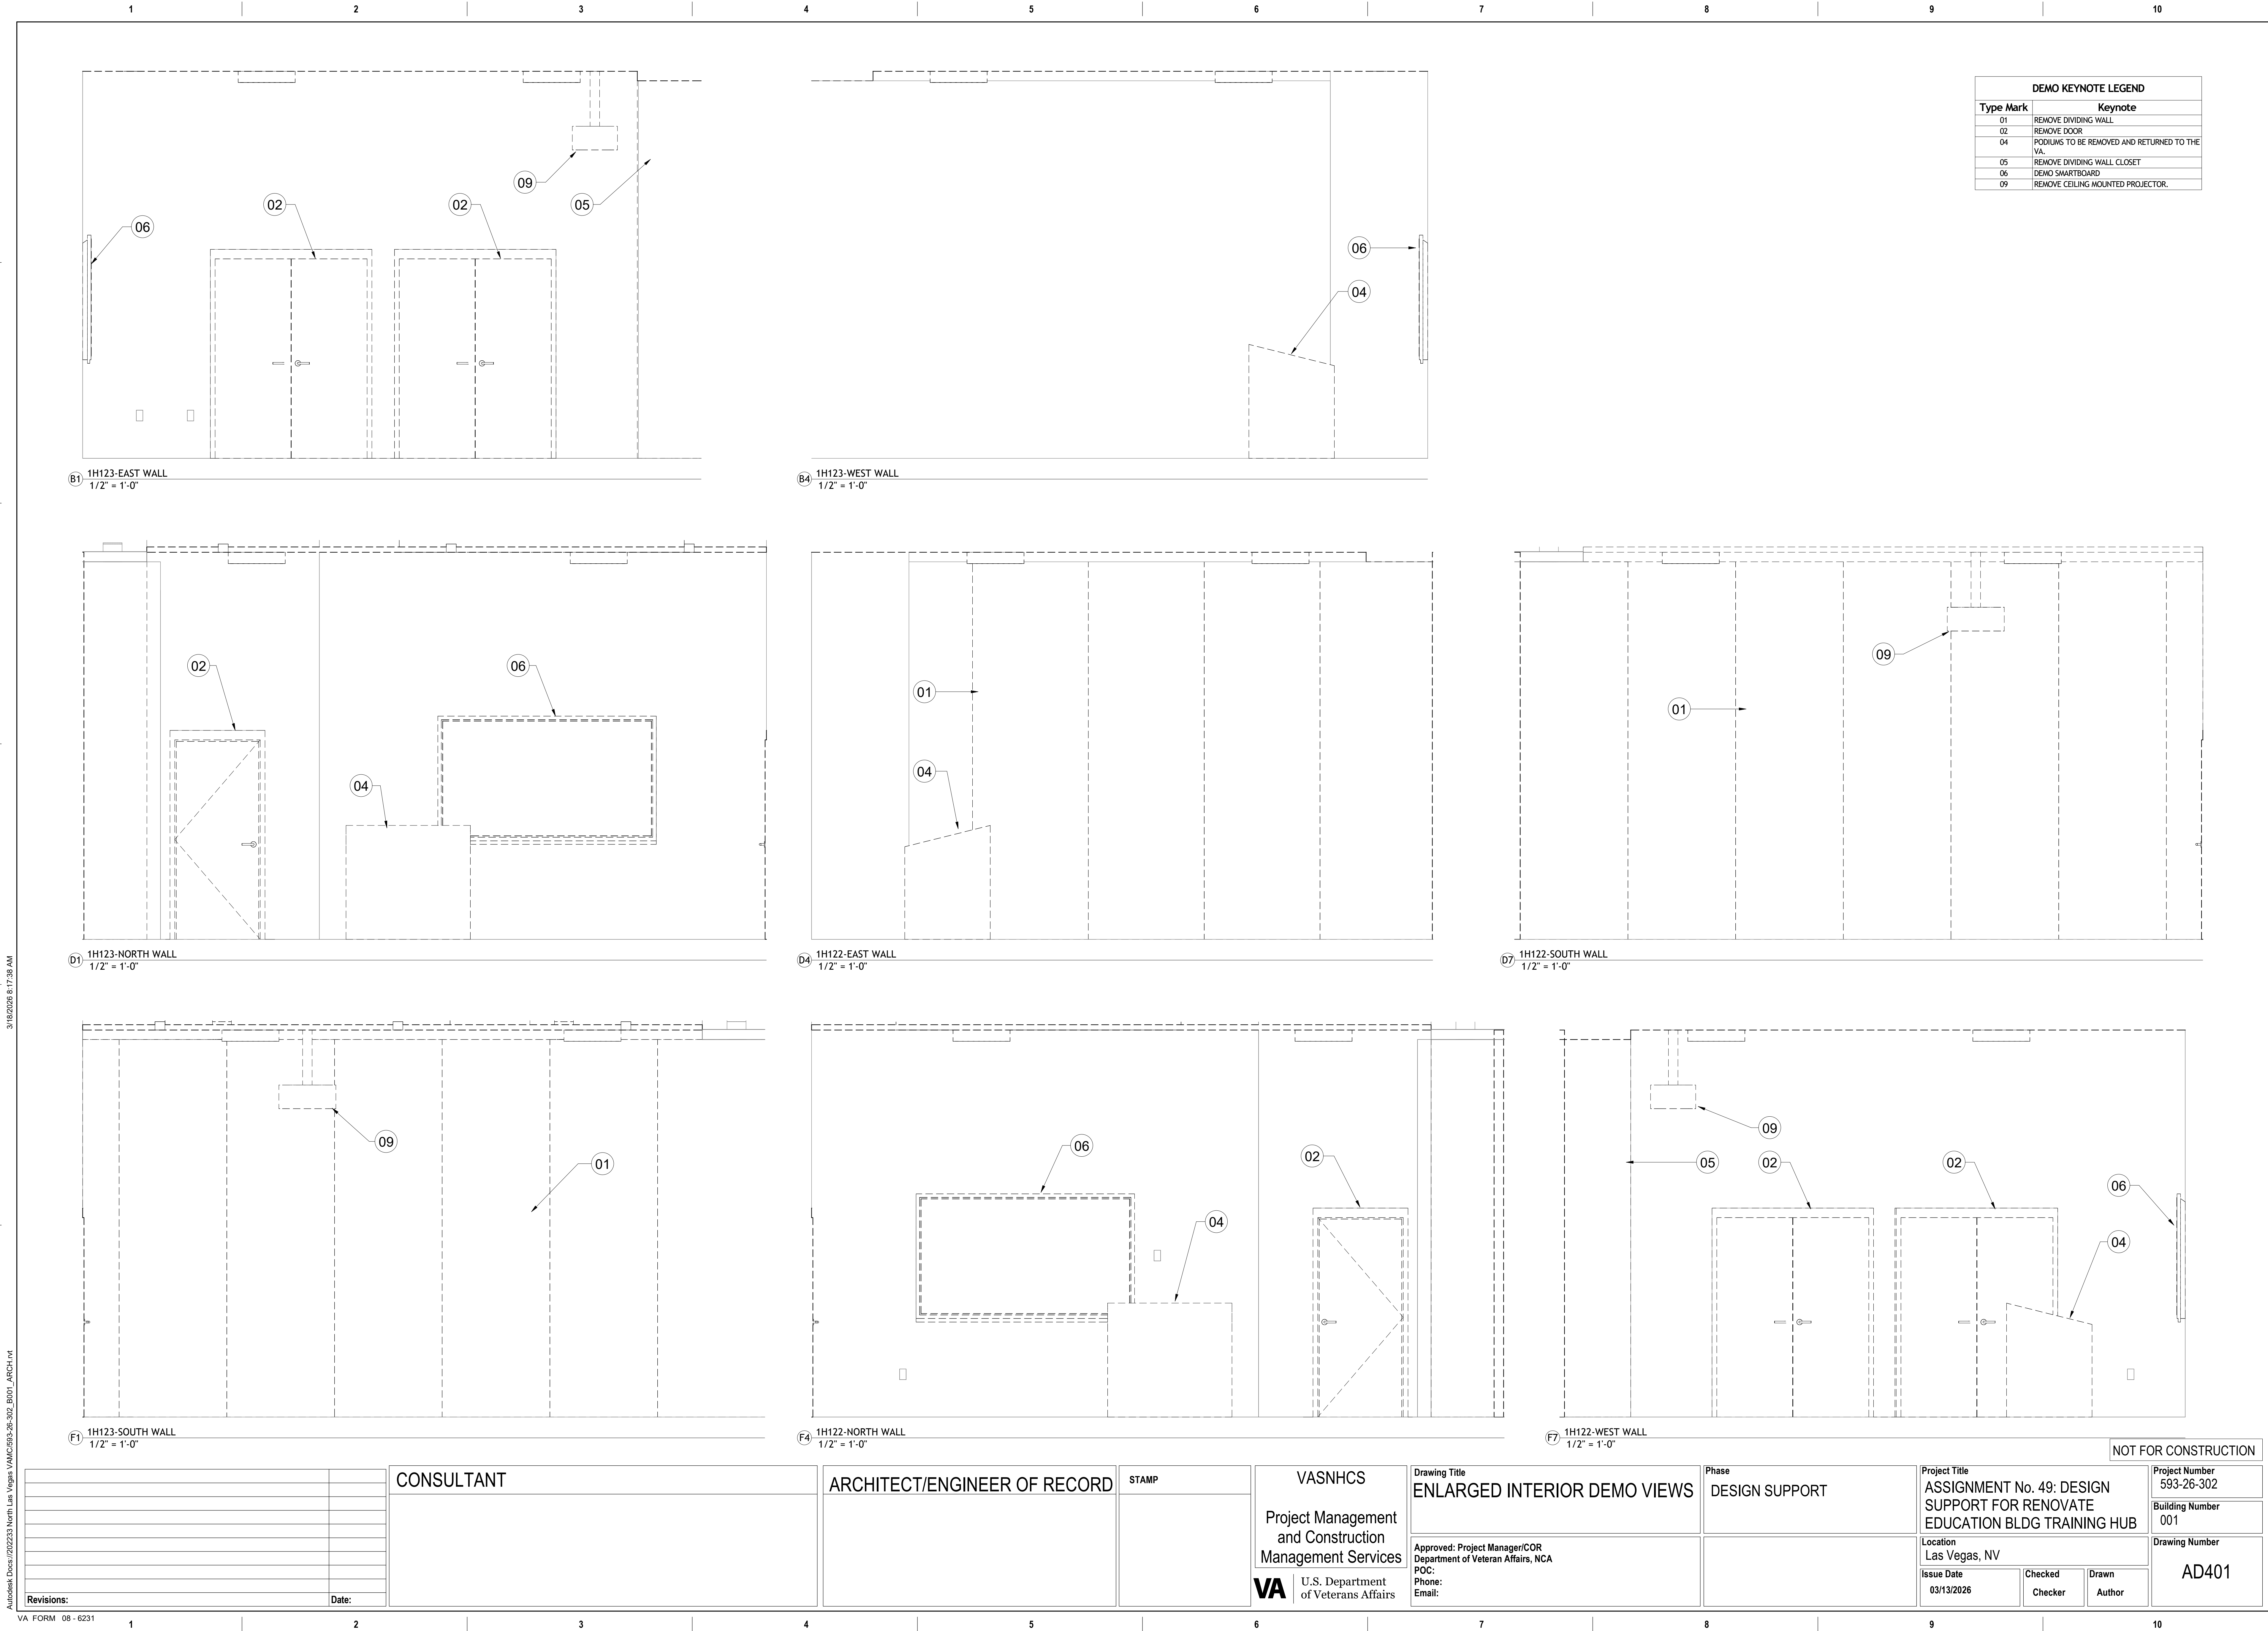

(B1) 1H125-EAST WALL
1/2" = 1'-0"

B4 1H125-WEST WALL
1/2" = 1'-0"

(D1) 1H125-NORTH WALL
1/2" = 1'-0"

D4 1H124-EAST WALL
1/2" = 1'-0"

(D7) 1H124-SOUTH WALL
1/2" = 1'-0"

(F1) 1H125-SOUTH WALL
1/2" = 1'-0"

F4 1H124-NORTH WALL
1/2" = 1'-0"

(F7) 1H124-WEST WALL
1/2" = 1'-0"

DEMO KEYNOTE LEGEND	
Type Mark	Keynote
01	REMOVE DIVIDING WALL.
02	REMOVE DOOR
04	PODIUMS TO BE REMOVED AND RETURNED TO THE VA.
05	REMOVE DIVIDING WALL CLOSET
06	DEMO SMARTBOARD
09	REMOVE CEILING MOUNTED PROJECTOR.

[illegible]

CONSULTANT

ARCHITECT/ENGINEER OF RECORD

STAMP

VASNHCS

Project Management
and Construction
Management Services

VA | U.S. Department
of Veterans Affairs

	Drawing Title
1	...
2	...
ENLARGED INTERIOR DEMO VIEWS

Approved: Project Manager/COR
Department of Veteran Affairs, NCA
POC:
Phone:
Email:

	Phase
1	Phase 1
2	Phase 2
3	Phase 3
100	Phase 100

DESIGN SUPPORT

Project Title

ASSIGNMENT No. 49: DESIGN
SUPPORT FOR RENOVATE
EDUCATION BLDG TRAINING HUB

Location	Las Vegas, NV
----------	---------------

Issue Date	03/13/2026
------------	------------

Checked
Checker

Drawn

Author

Project Number
500 00 000


593-26-302

Building Number
001

Drawing Number

AD402

NOT FOR CONSTRUCTION

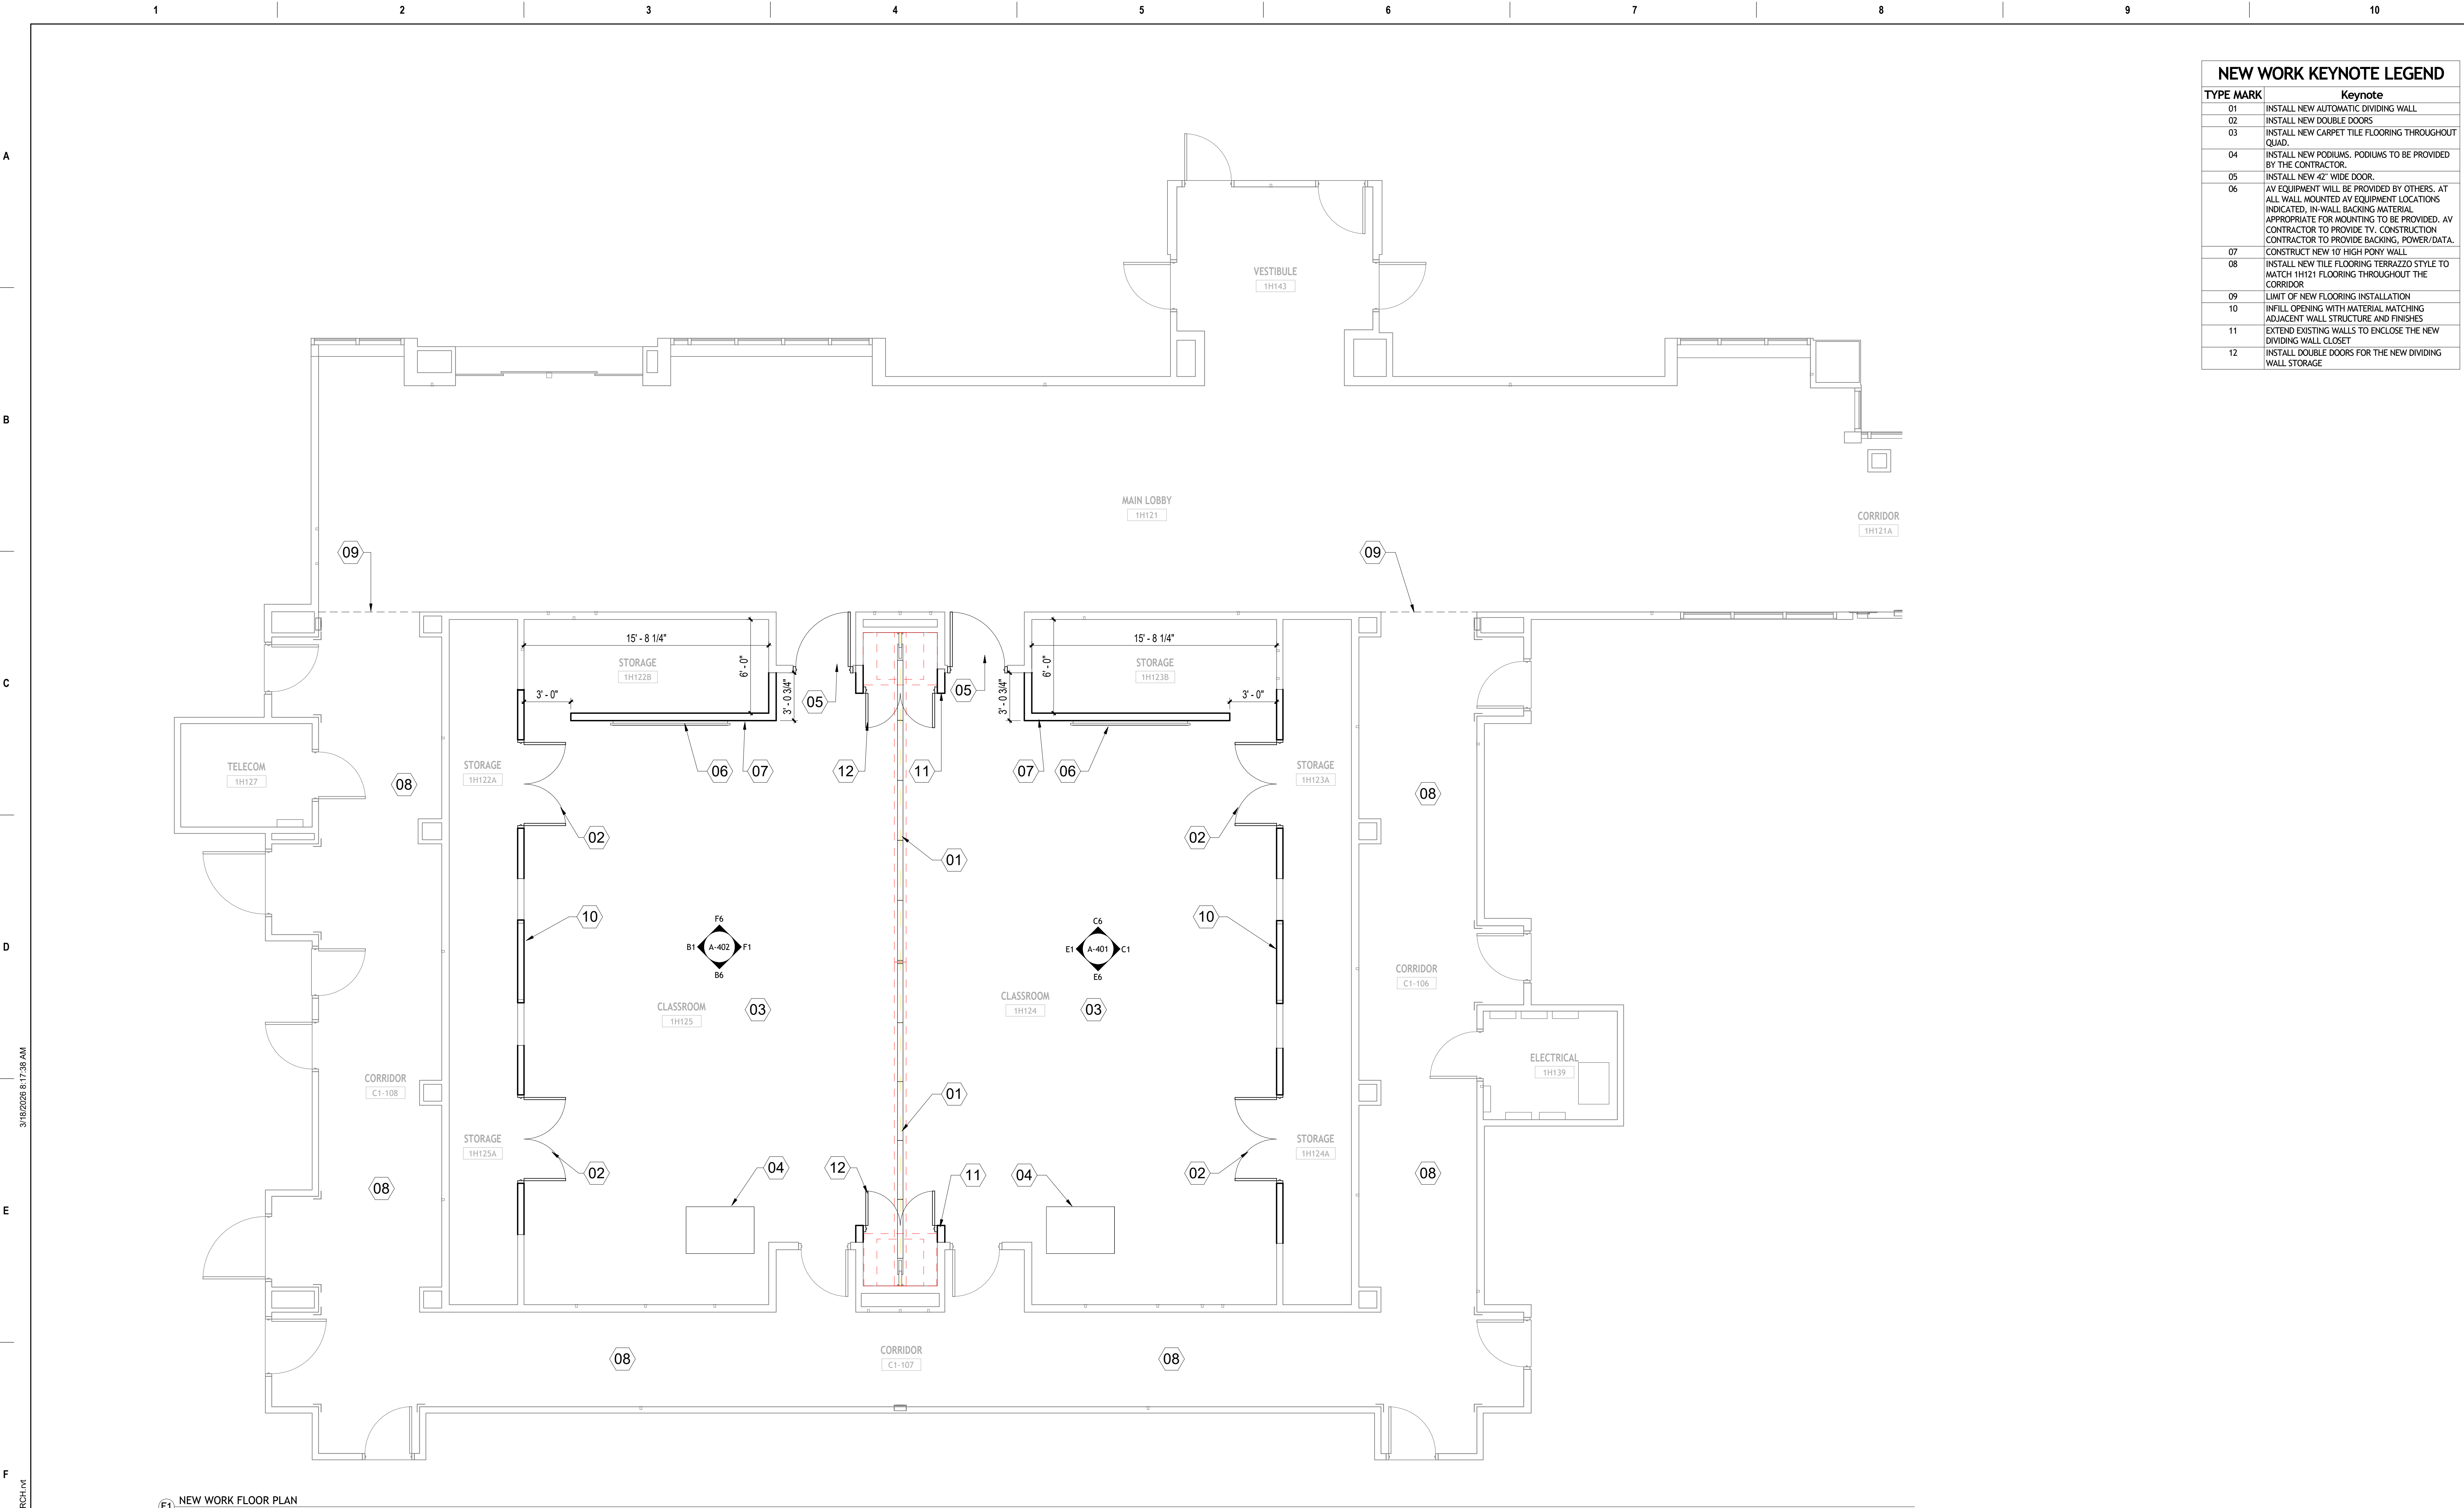

NEW WORK KEYNOTE LEGEND	
TYPE MARK	Keynote
01	INSTALL NEW AUTOMATIC DIVIDING WALL
02	INSTALL NEW DOUBLE DOORS
03	INSTALL NEW CARPET TILE FLOORING THROUGHOUT QUAD.
04	INSTALL NEW PODIUMS. PODIUMS TO BE PROVIDED BY THE CONTRACTOR.
05	INSTALL NEW 42" WIDE DOOR.
06	AV EQUIPMENT WILL BE PROVIDED BY OTHERS. AT ALL WALL MOUNTED AV EQUIPMENT LOCATIONS INDICATED, IN-WALL BACKING MATERIAL APPROPRIATE FOR MOUNTING TO BE PROVIDED. AV CONTRACTOR TO PROVIDE TV. CONSTRUCTION CONTRACTOR TO PROVIDE BACKING, POWER/DATA.
07	CONSTRUCT NEW 10' HIGH PONY WALL
08	INSTALL NEW TILE FLOORING TERRAZZO STYLE TO MATCH 1H121 FLOORING THROUGHOUT THE CORRIDOR
09	LIMIT OF NEW FLOORING INSTALLATION
10	INFILL OPENING WITH MATERIAL MATCHING ADJACENT WALL STRUCTURE AND FINISHES
11	EXTEND EXISTING WALLS TO ENCLOSE THE NEW DIVIDING WALL CLOSET
12	INSTALL DOUBLE DOORS FOR THE NEW DIVIDING WALL STORAGE


F1 NEW WORK FLOOR PLAN
1/4" = 1'-0"

NOT FOR CONSTRUCTION

		CONSULTANT	ARCHITECT/ENGINEER OF RECORD	STAMP	VASNHCS Project Management and Construction Management Services VA U.S. Department of Veterans Affairs	Drawing Title NEW WORK FLOOR PLAN Approved: Project Manager/COR Department of Veteran Affairs, NCA POC: Phone: Email:	Phase DESIGN SUPPORT	Project Title ASSIGNMENT No. 49: DESIGN SUPPORT FOR RENOVATE EDUCATION BLDG TRAINING HUB	Location Las Vegas, NV	Project Number 593-26-302 Building Number 001 Drawing Number A-101
Revisions:	Date:									
								Issue Date 03/13/2026	Checked Checker	Drawn Author

3/18/2026 8:17:38 AM
VA FORM 08 - 6231
Autodesk Docs/202223 North Las Vegas VAMC/593-26-302_B001_ARCH.rvt

NEW WORK KEYNOTE LEGEND	
TYPE MARK	Keynote
13	INSTALL NEW CEILING TILE AND GRID.
14	INSTALL NEW SPOT LIGHT ABOVE PODIUM.

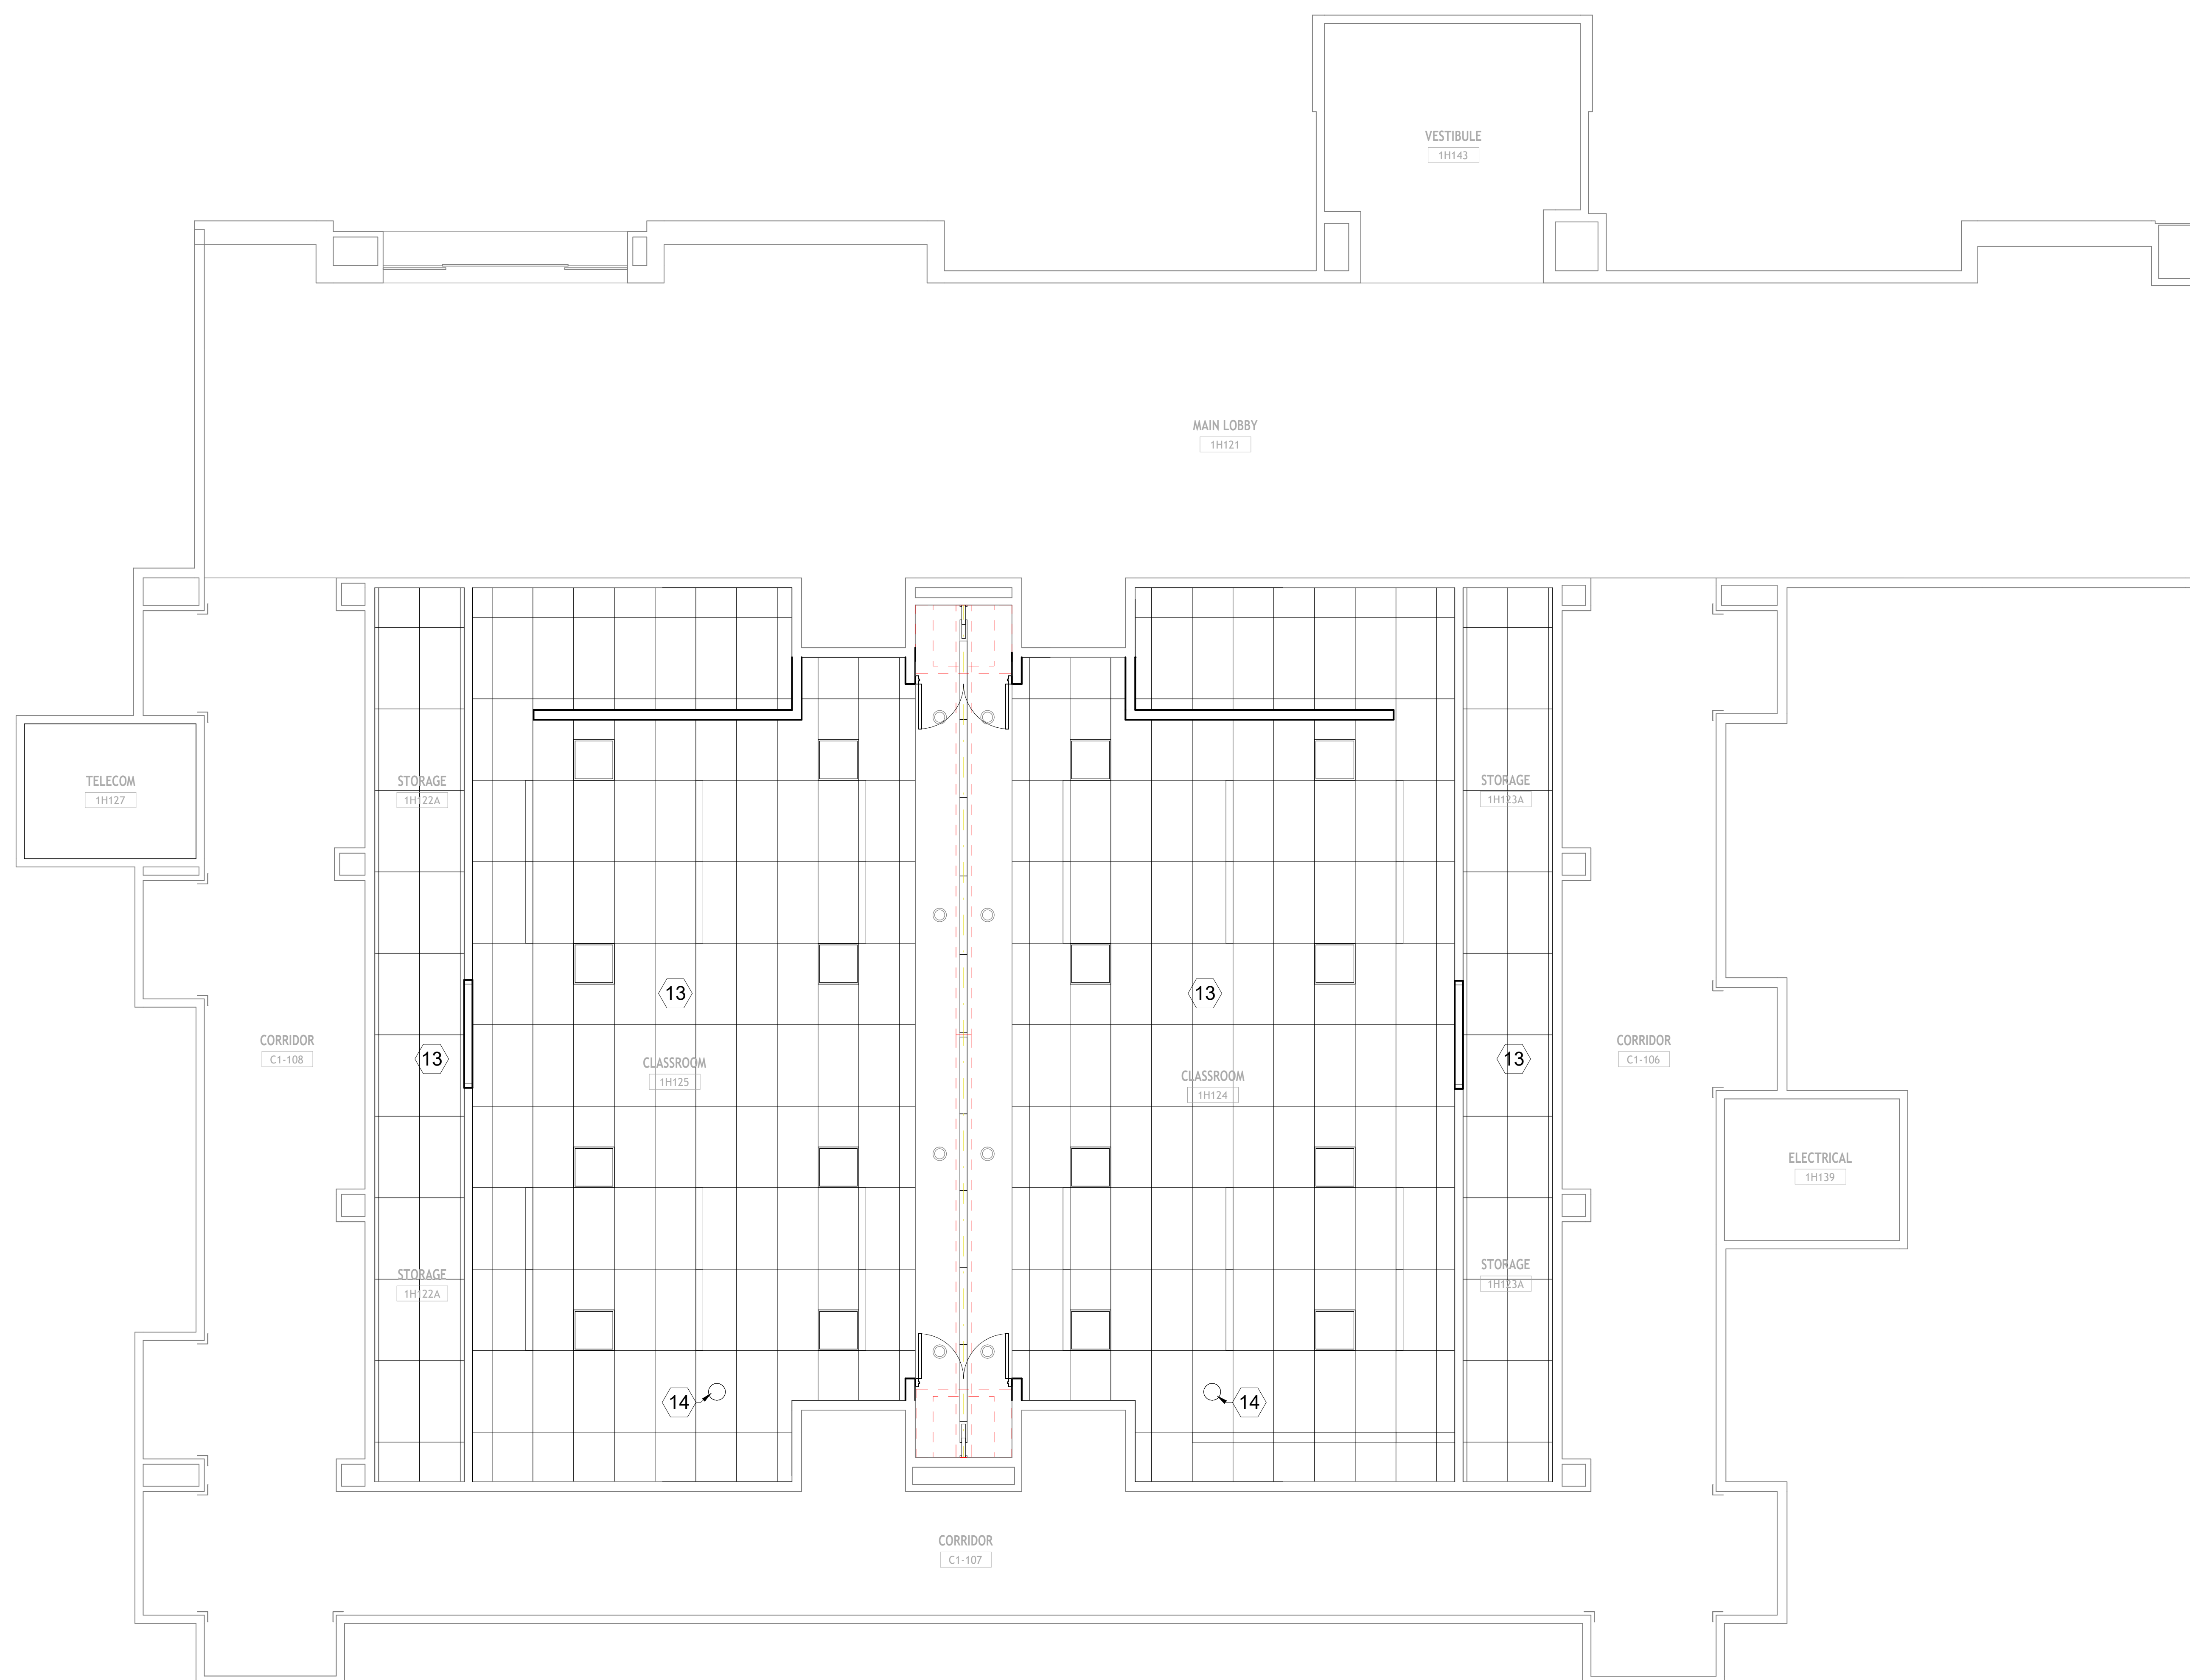


F1 NEW WORK REFLECTED CEILING PLAN
1/4" = 1'-0"

$$1/4'' = 1'-0''$$


NOT FOR CONSTRUCTION

		CONSULTANT	ARCHITECT/ENGINEER OF RECORD	STAMP	VASNHCS Project Management and Construction Management Services VA U.S. Department of Veterans Affairs	Drawing Title NEW WORK REFLECTED CEILING PLAN	Phase	DESIGN SUPPORT	Project Title ASSIGNMENT No. 49: DESIGN SUPPORT FOR RENOVATE EDUCATION BLDG TRAINING HUB	Project Number 593-26-302
						Building Number 001				
						Drawing Number A-102				
	Revisions:	Date:								

NEW WORK KEYNOTE LEGEND	
TYPE MARK	Keynote
01	INSTALL NEW AUTOMATIC DIVING WALL
02	INSTALL NEW DOUBLE DOORS
04	INSTALL NEW PODIUMS. PODIUMS TO BE PROVIDED BY THE CONTRACTOR.
05	INSTALL NEW 42" WIDE DOOR.
06	AV EQUIPMENT WILL BE PROVIDED BY OTHERS. ALL WALL MOUNTED AV EQUIPMENT LOCATIONS INDICATED. IN-WALL SACKING MATERIAL APPROPRIATE FOR MOUNTING TO BE PROVIDED. AV CONTRACTOR TO PROVIDE TV, CONSTRUCTION CONTRACTOR TO PROVIDE SACKING, POWER/DATA.
07	CONSTRUCT NEW 10' HIGH DIVING WALL
10	INFILL OPENING WITH MATERIAL MATCHING ADJACENT WALL STRUCTURE AND FINISHES
11	EXTEND EXISTING WALLS TO ENCLOSE THE NEW DIVING WALL CLOSET
12	INSTALL DOUBLE DOORS FOR THE NEW DIVING WALL STORAGE
14	INSTALL NEW SPOT LIGHT ABOVE PODIUM

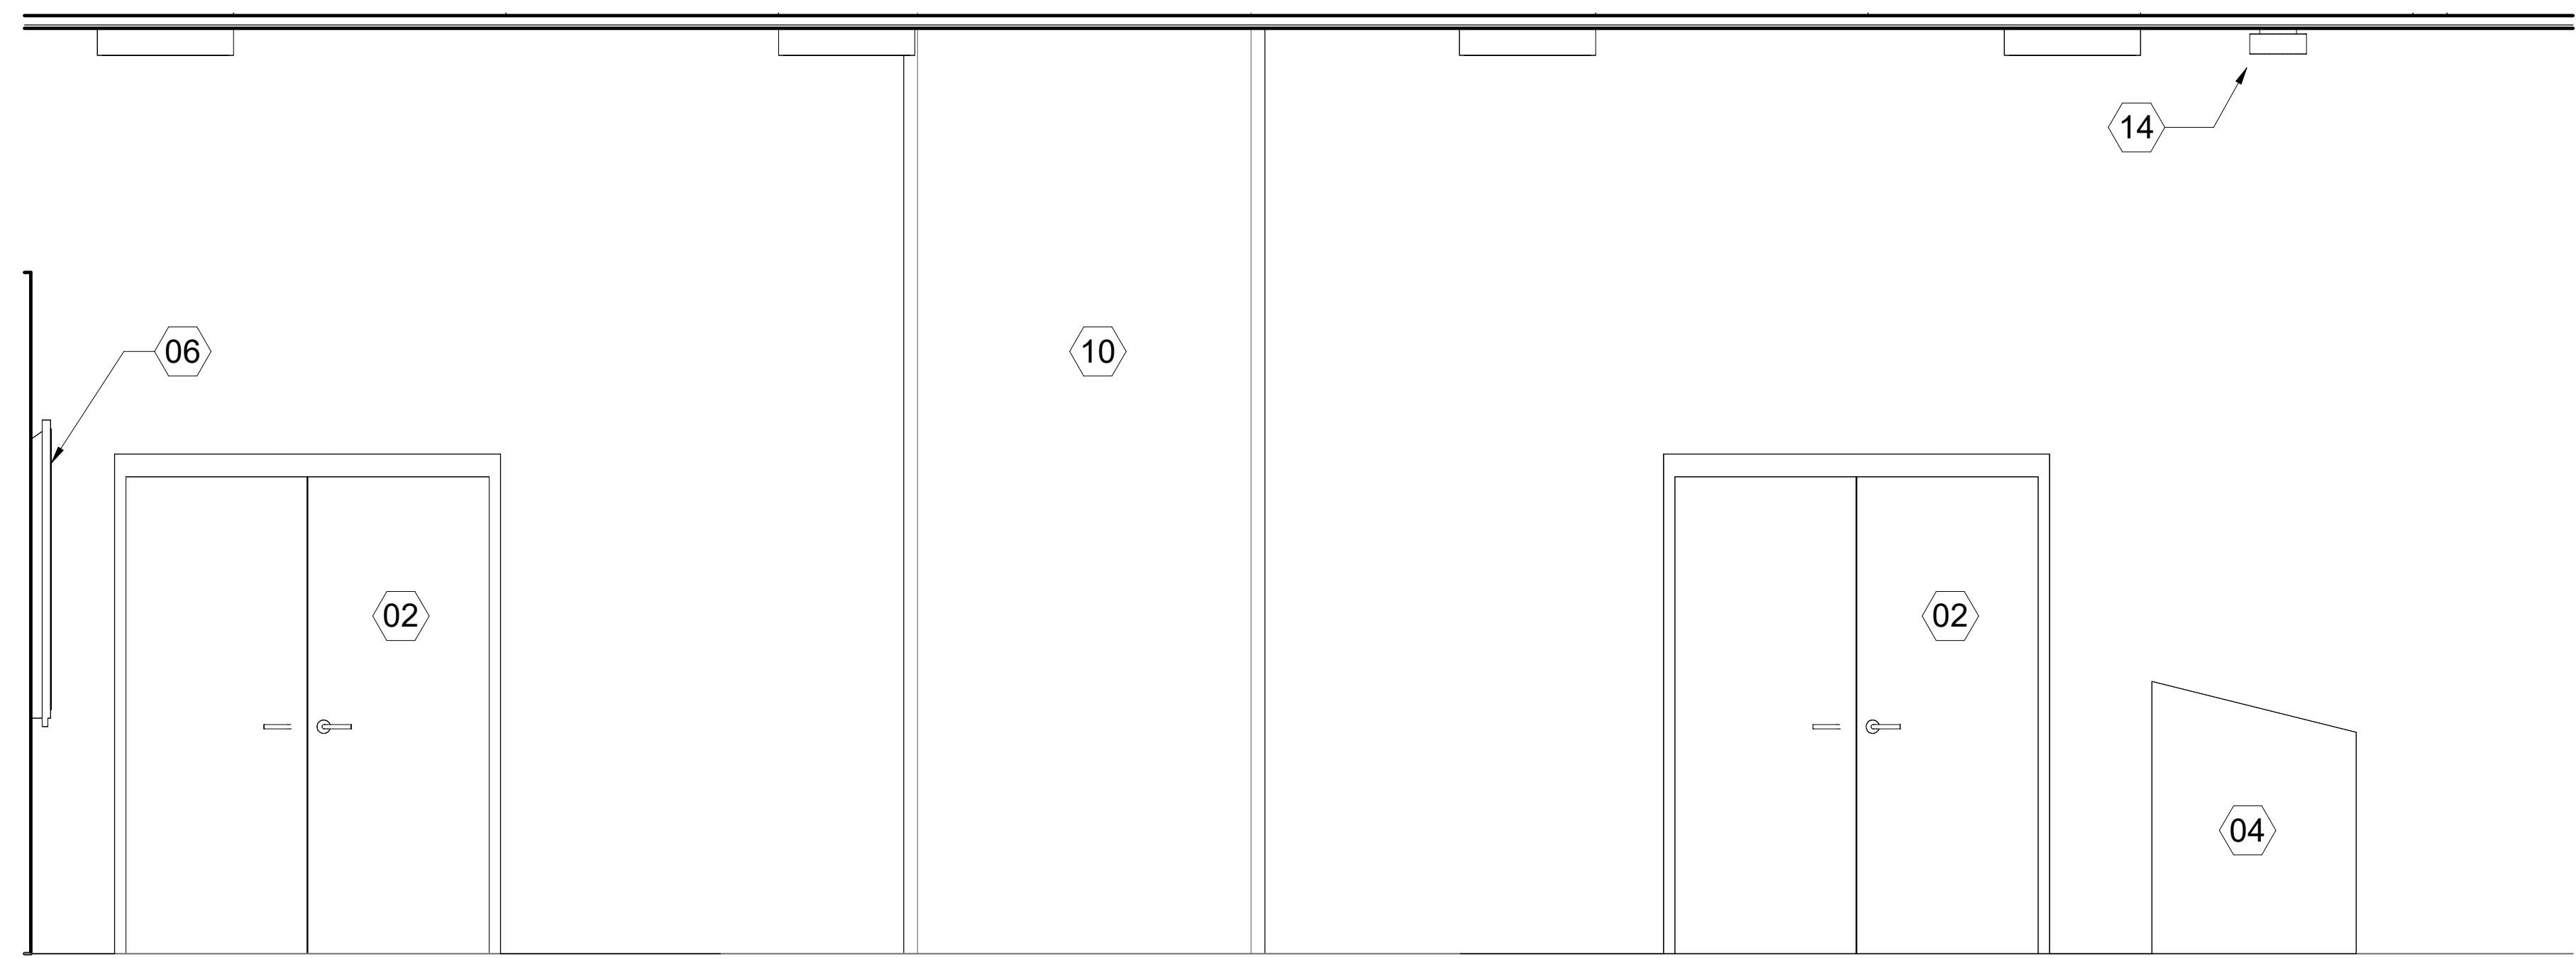


1H123-EAST ELEVATION
1/2" = 1'-0"

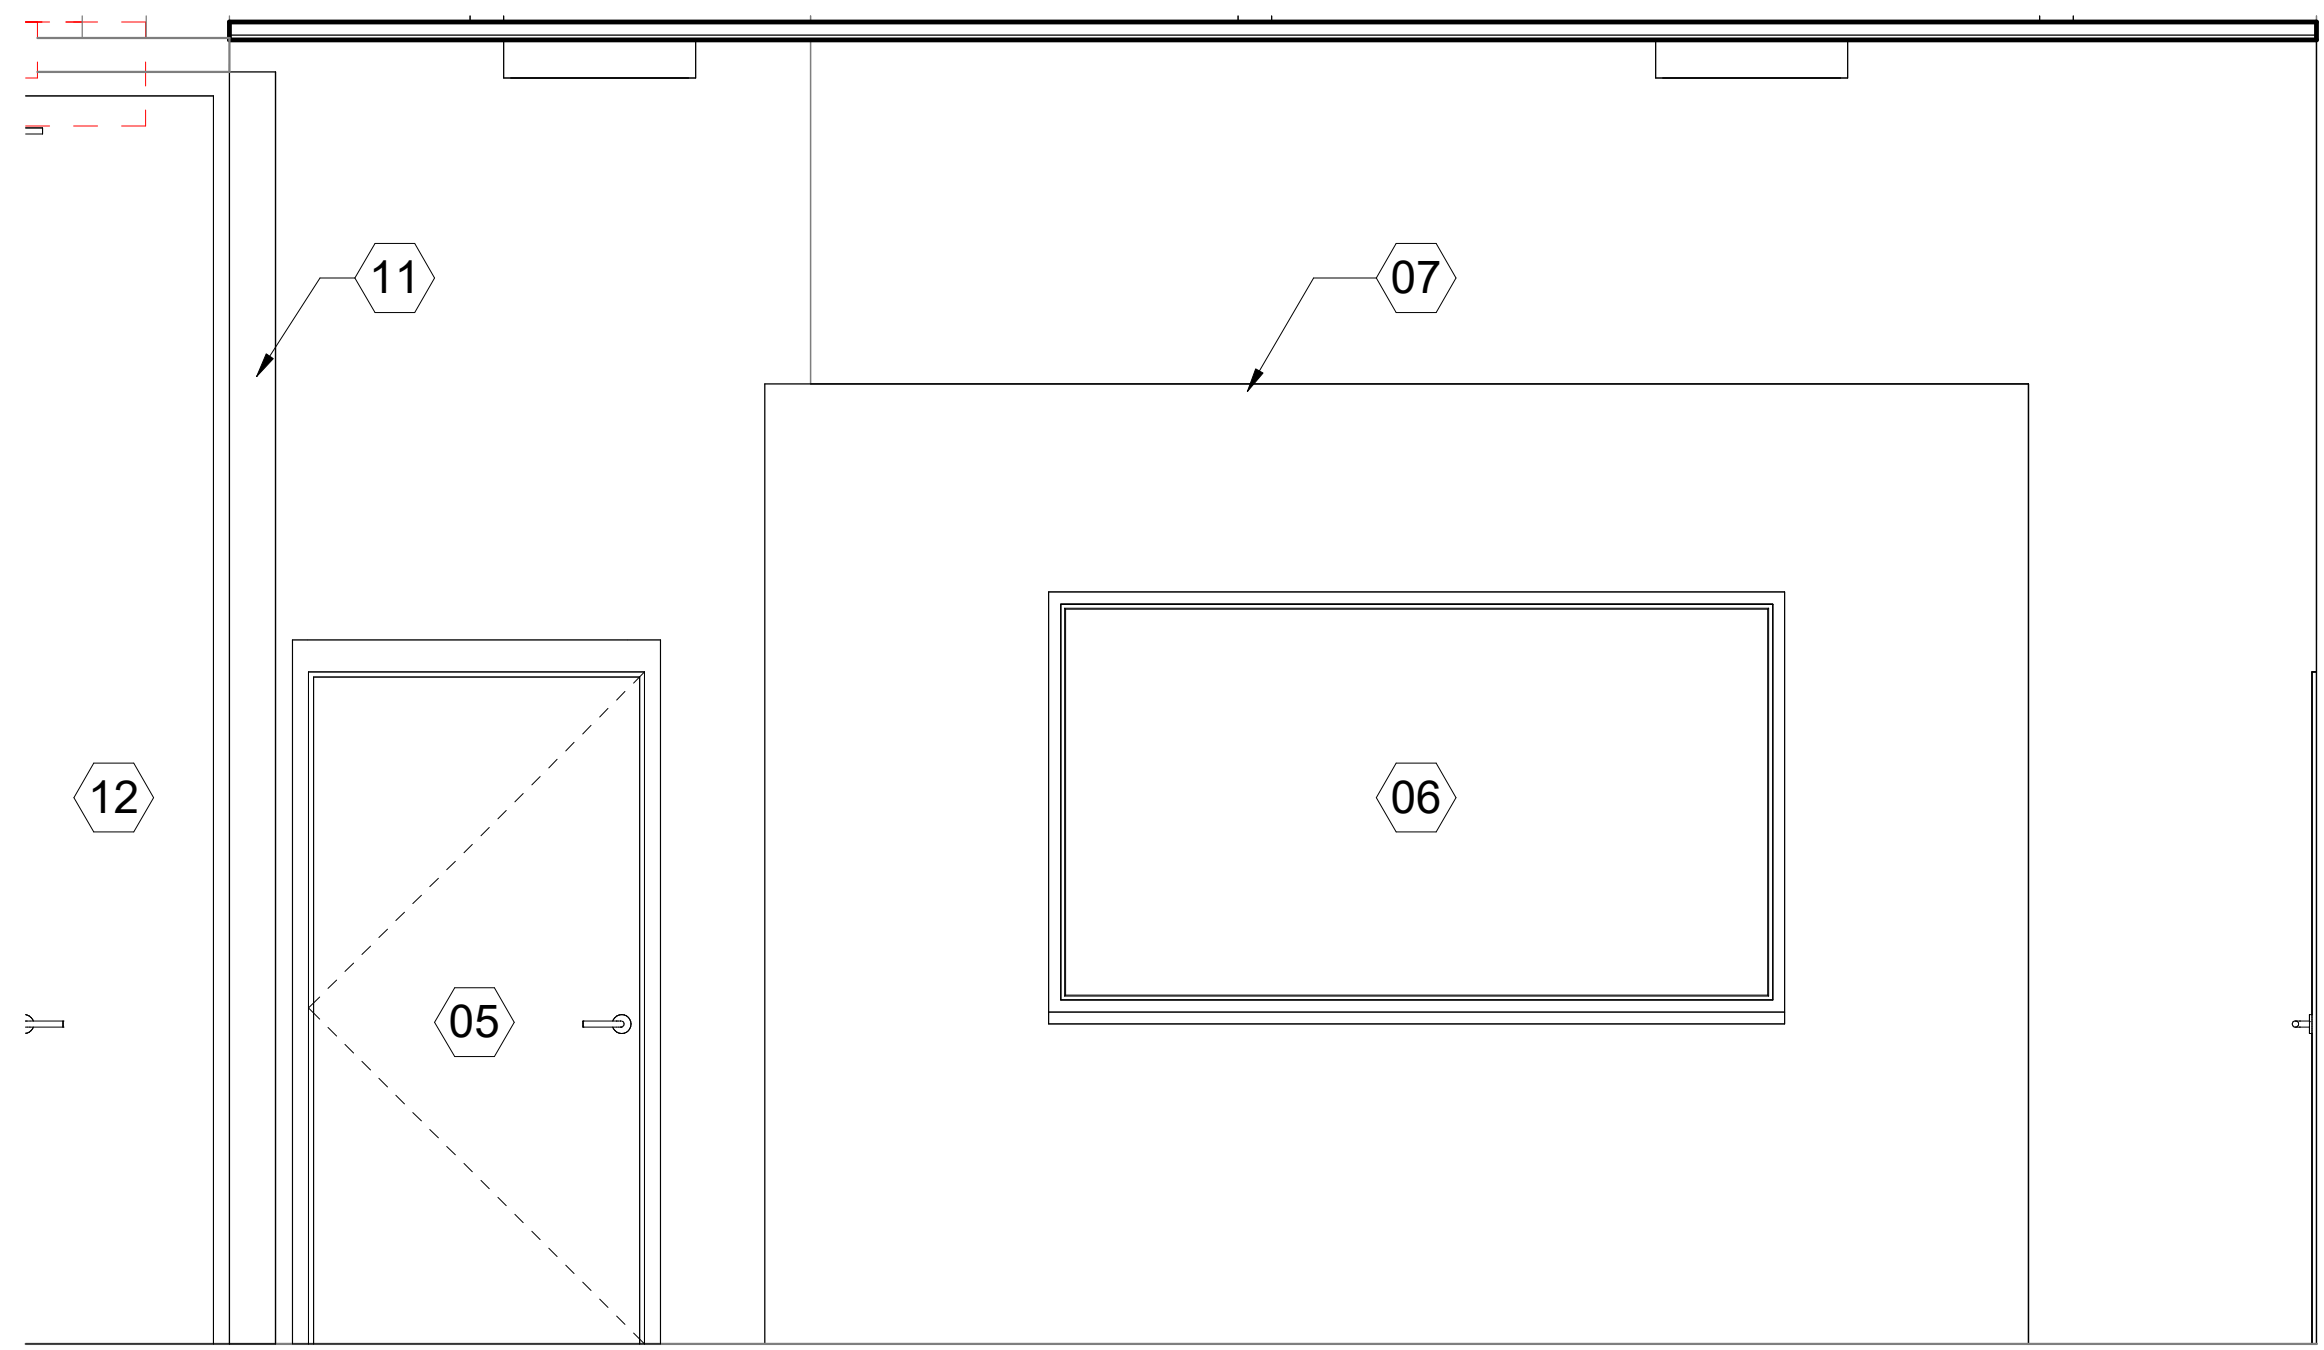

C6 1H123-NORTH ELEVATION
1/2" = 1'-0"

(E1) 1H123-WEST ELEVATION
1/2" = 1'-0"

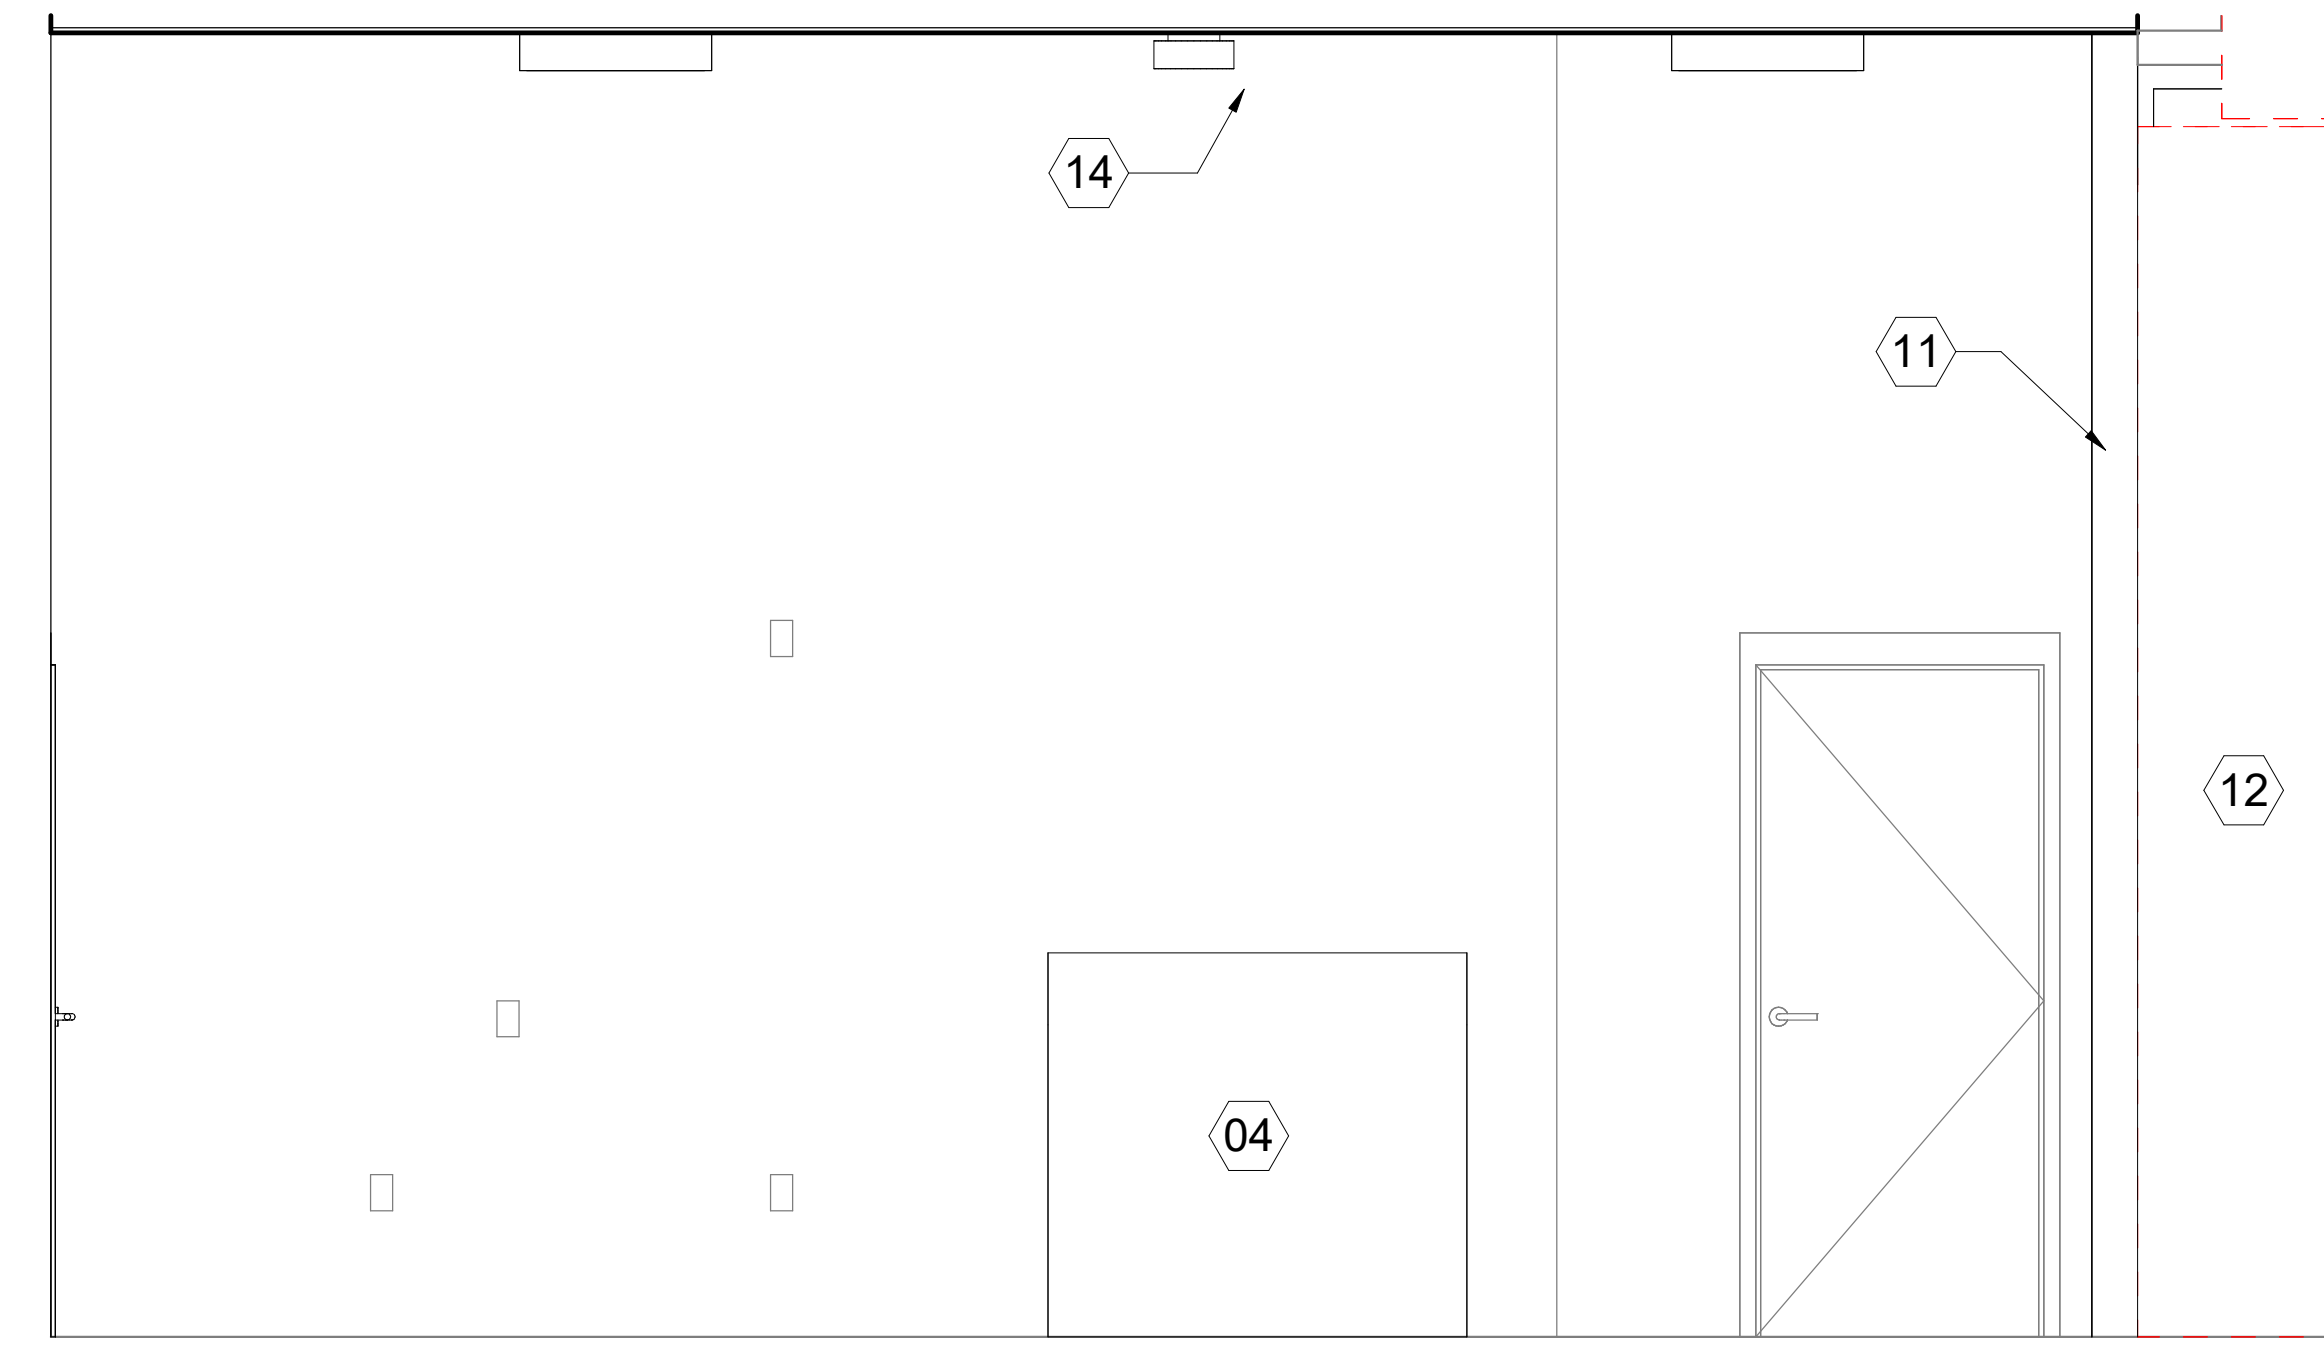

E6 1H123-SOUTH ELEVATION
1/2" = 1'-0"

[illegible]

CONSULTANT

ARCHITECT/ENGINEER OF RECORD

STAMP

VASNHCS

Project Management
and Construction
Management Services

VA | U.S. Department
of Veterans Affairs

	Drawing Title
--	----------------------

NEW WORK ENLARGED INTERIOR
VIEWS

Approved: Project Manager/COR
Department of Veteran Affairs, NCA
POC:
Phone:
Email:

Phase

DESIGN SUPPORT

Project Title	
---------------	--

ASSIGNMENT No. 49: DESIGN
SUPPORT FOR RENOVATE
EDUCATION BLDG TRAINING HUB

Location	Las Vegas, NV
----------	---------------

Issue Date	03/13/2026
------------	------------

Checked
Checker

Drawn	
Author	

Project Number
593-26-302

Building Number	001
-----------------	-----

Drawing Number


A-401

3/18/2026 8:17:40 AM


Autodesk Docs://202233 North Las Vegas VAMC/593-26-302_B001_ARCH.m

VA FORM 08-6231


NEW WORK KEYNOTE LEGEND	
TYPE MARK	Keynote
01	INSTALL NEW AUTOMATIC DIVIDING WALL
02	INSTALL NEW DOUBLE DOORS
04	INSTALL NEW PODIUMS. PODIUMS TO BE PROVIDED BY THE CONTRACTOR
05	INSTALL NEW 42" WIDE DOOR.
06	AV EQUIPMENT WILL BE PROVIDED BY OTHERS. AT ALL WALL MOUNTED AV EQUIPMENT LOCATIONS INSTALLED, IN-WALL BASKET MOUNTING APPROPRIATE FOR MOUNTING TO BE PROVIDED, AV CONTRACTOR TO PROVIDE TV, CONSTRUCTION CONTRACTOR TO PROVIDE BASKETING, POWER/DATA.
07	CONSTRUCT NEW 10' HIGH-PONY WALL
10	INFILL ADJACENT WITH MATERIAL MATCHING EXISTING WALL STRUCTURE AND FINISHES
11	EXTEND EXISTING WALLS TO ENCLOSE THE NEW DIVIDING WALL CLOSET
12	INSTALL DOUBLE DOORS FOR THE NEW DIVIDING WALL STORAGE
14	INSTALL NEW SPOT LIGHT ABOVE PODIUM

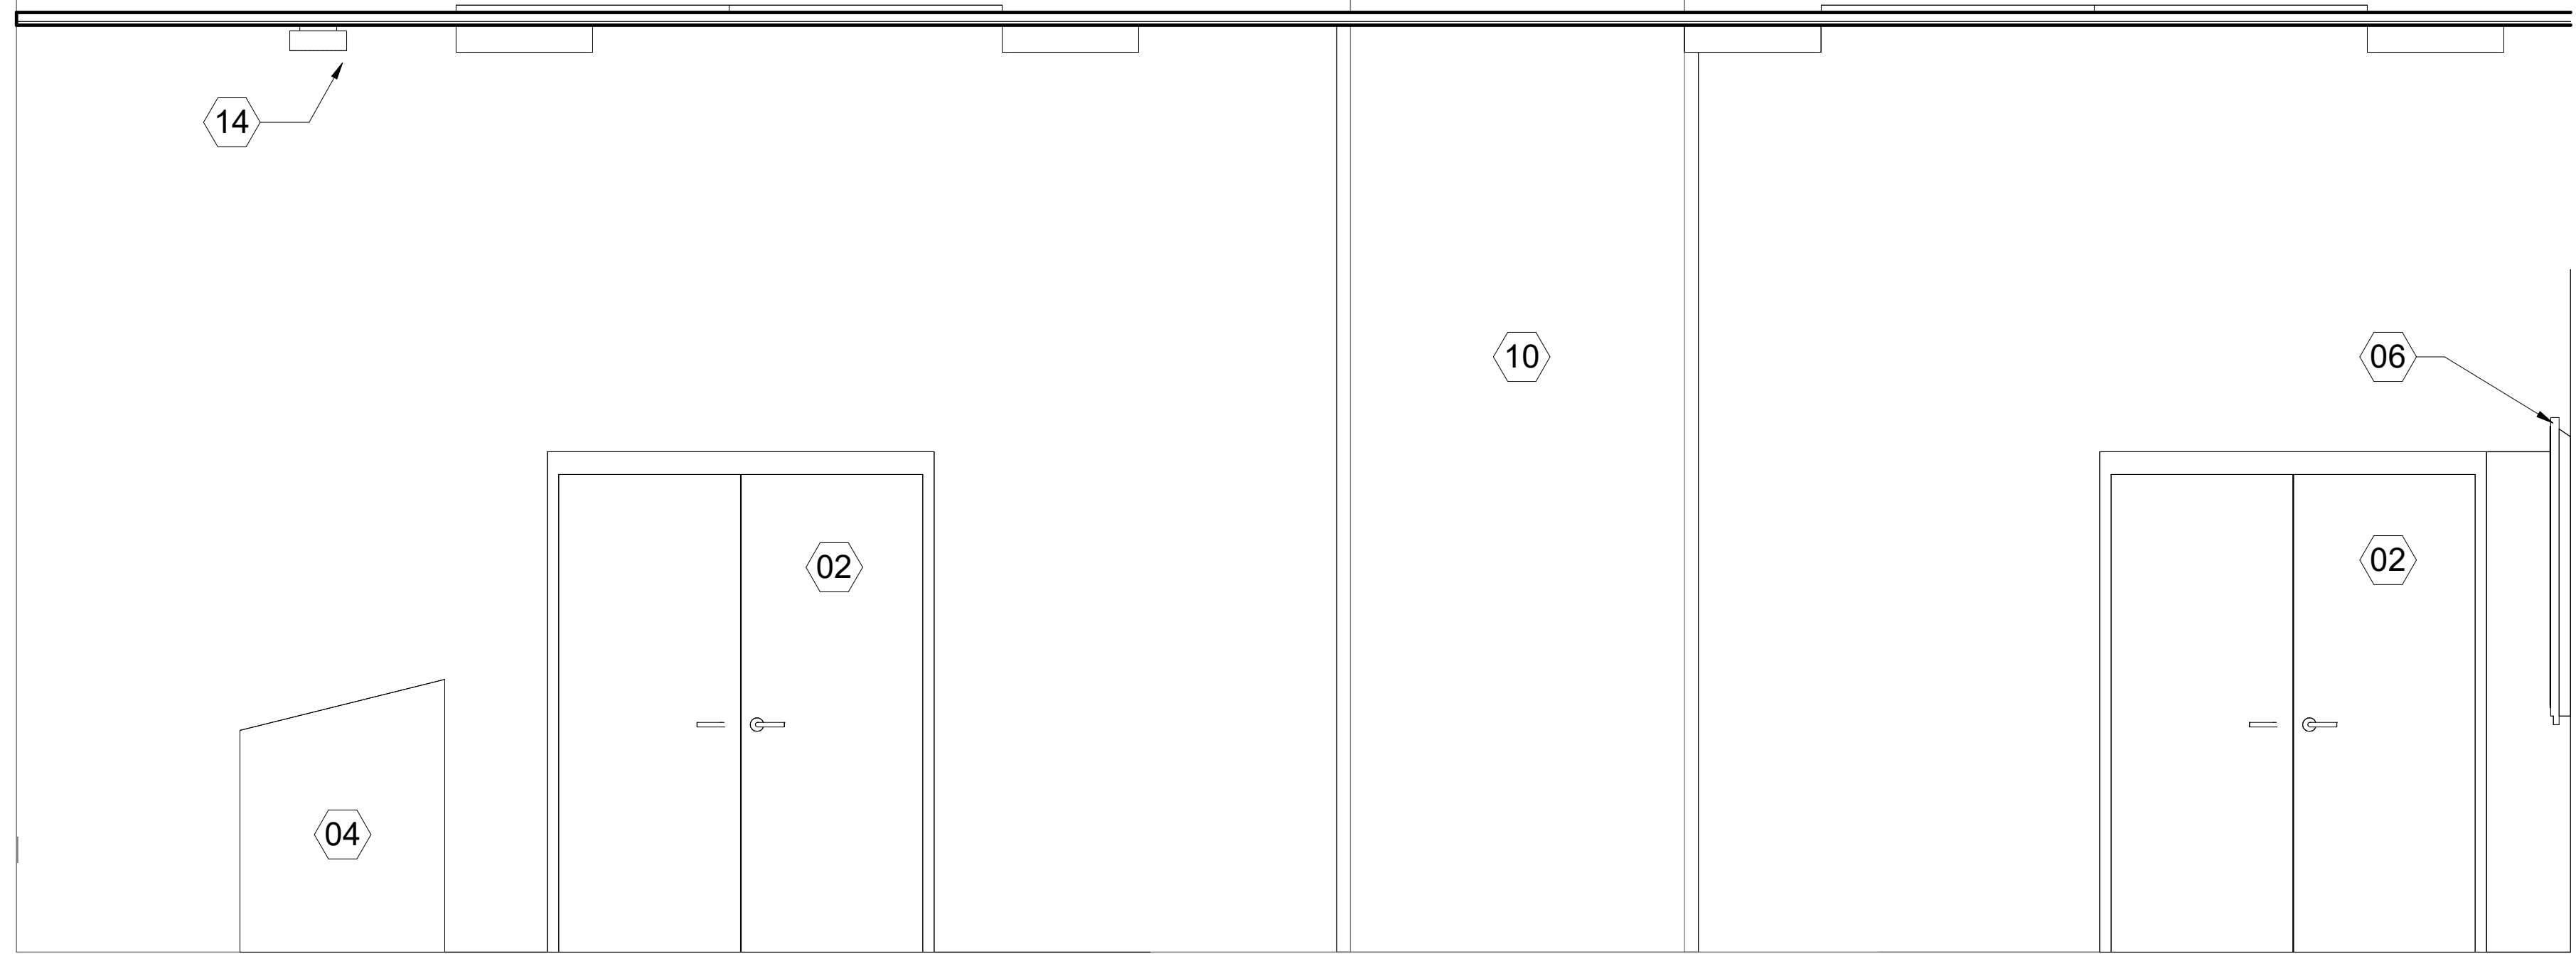


(B1) 1H122-WEST ELEVATION
1/2" = 1'-0"

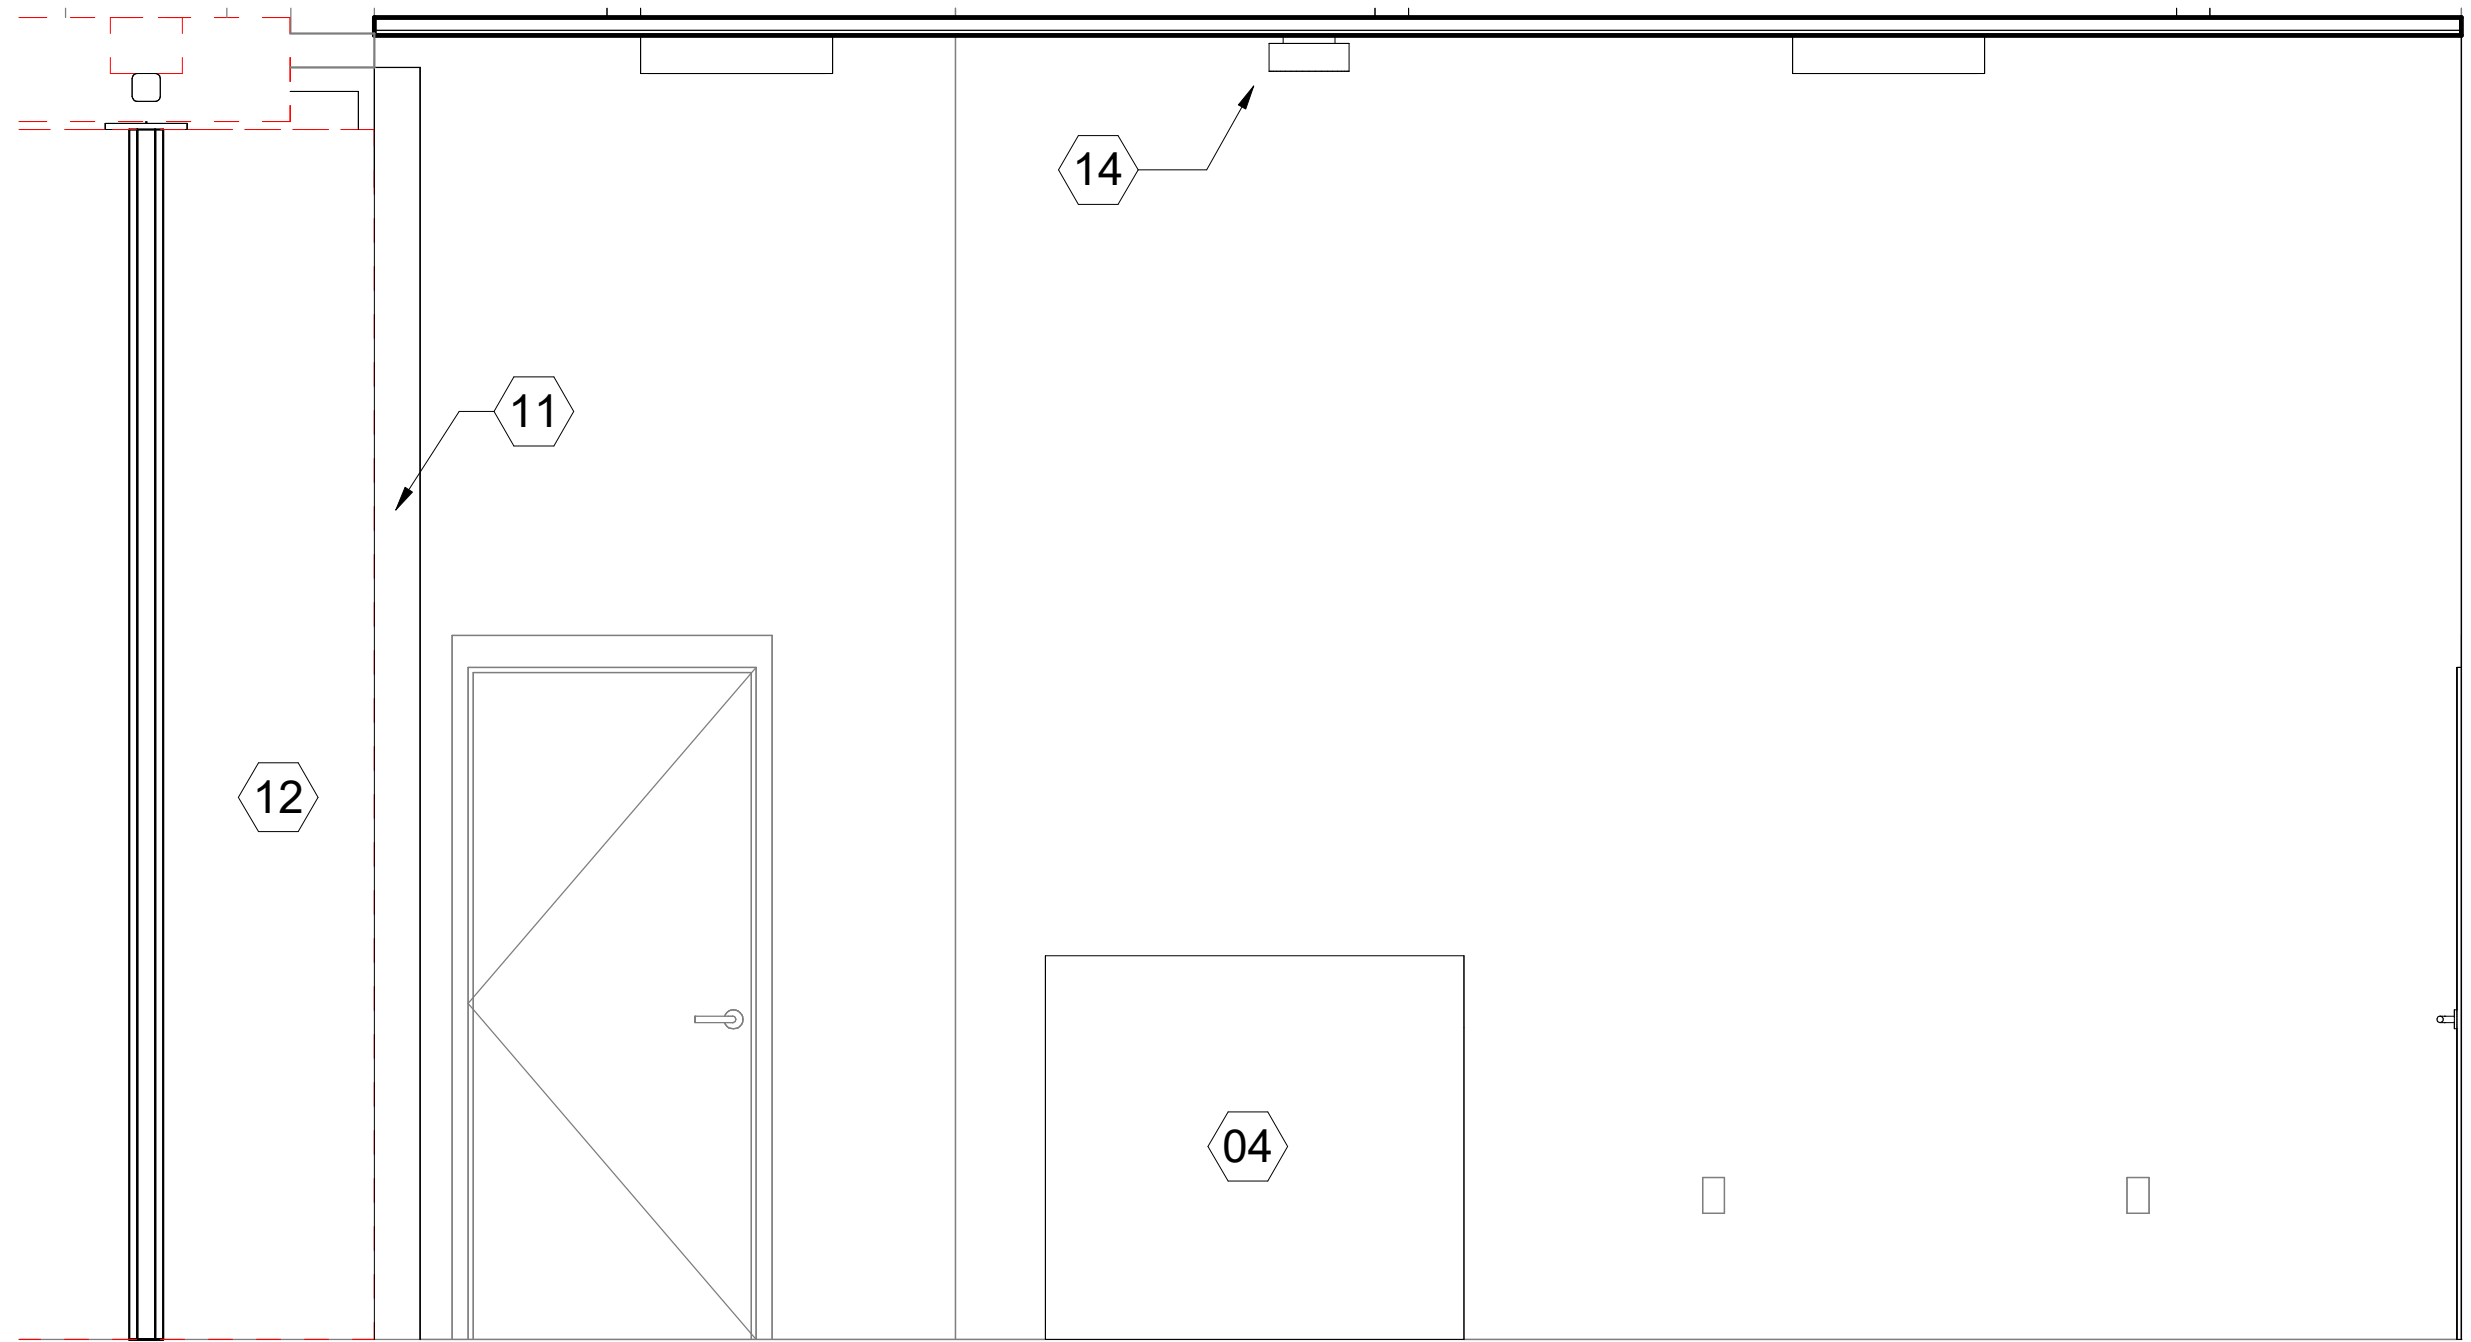

(B6) 1H122-SOUTH ELEVATION
1/2" = 1'-0"

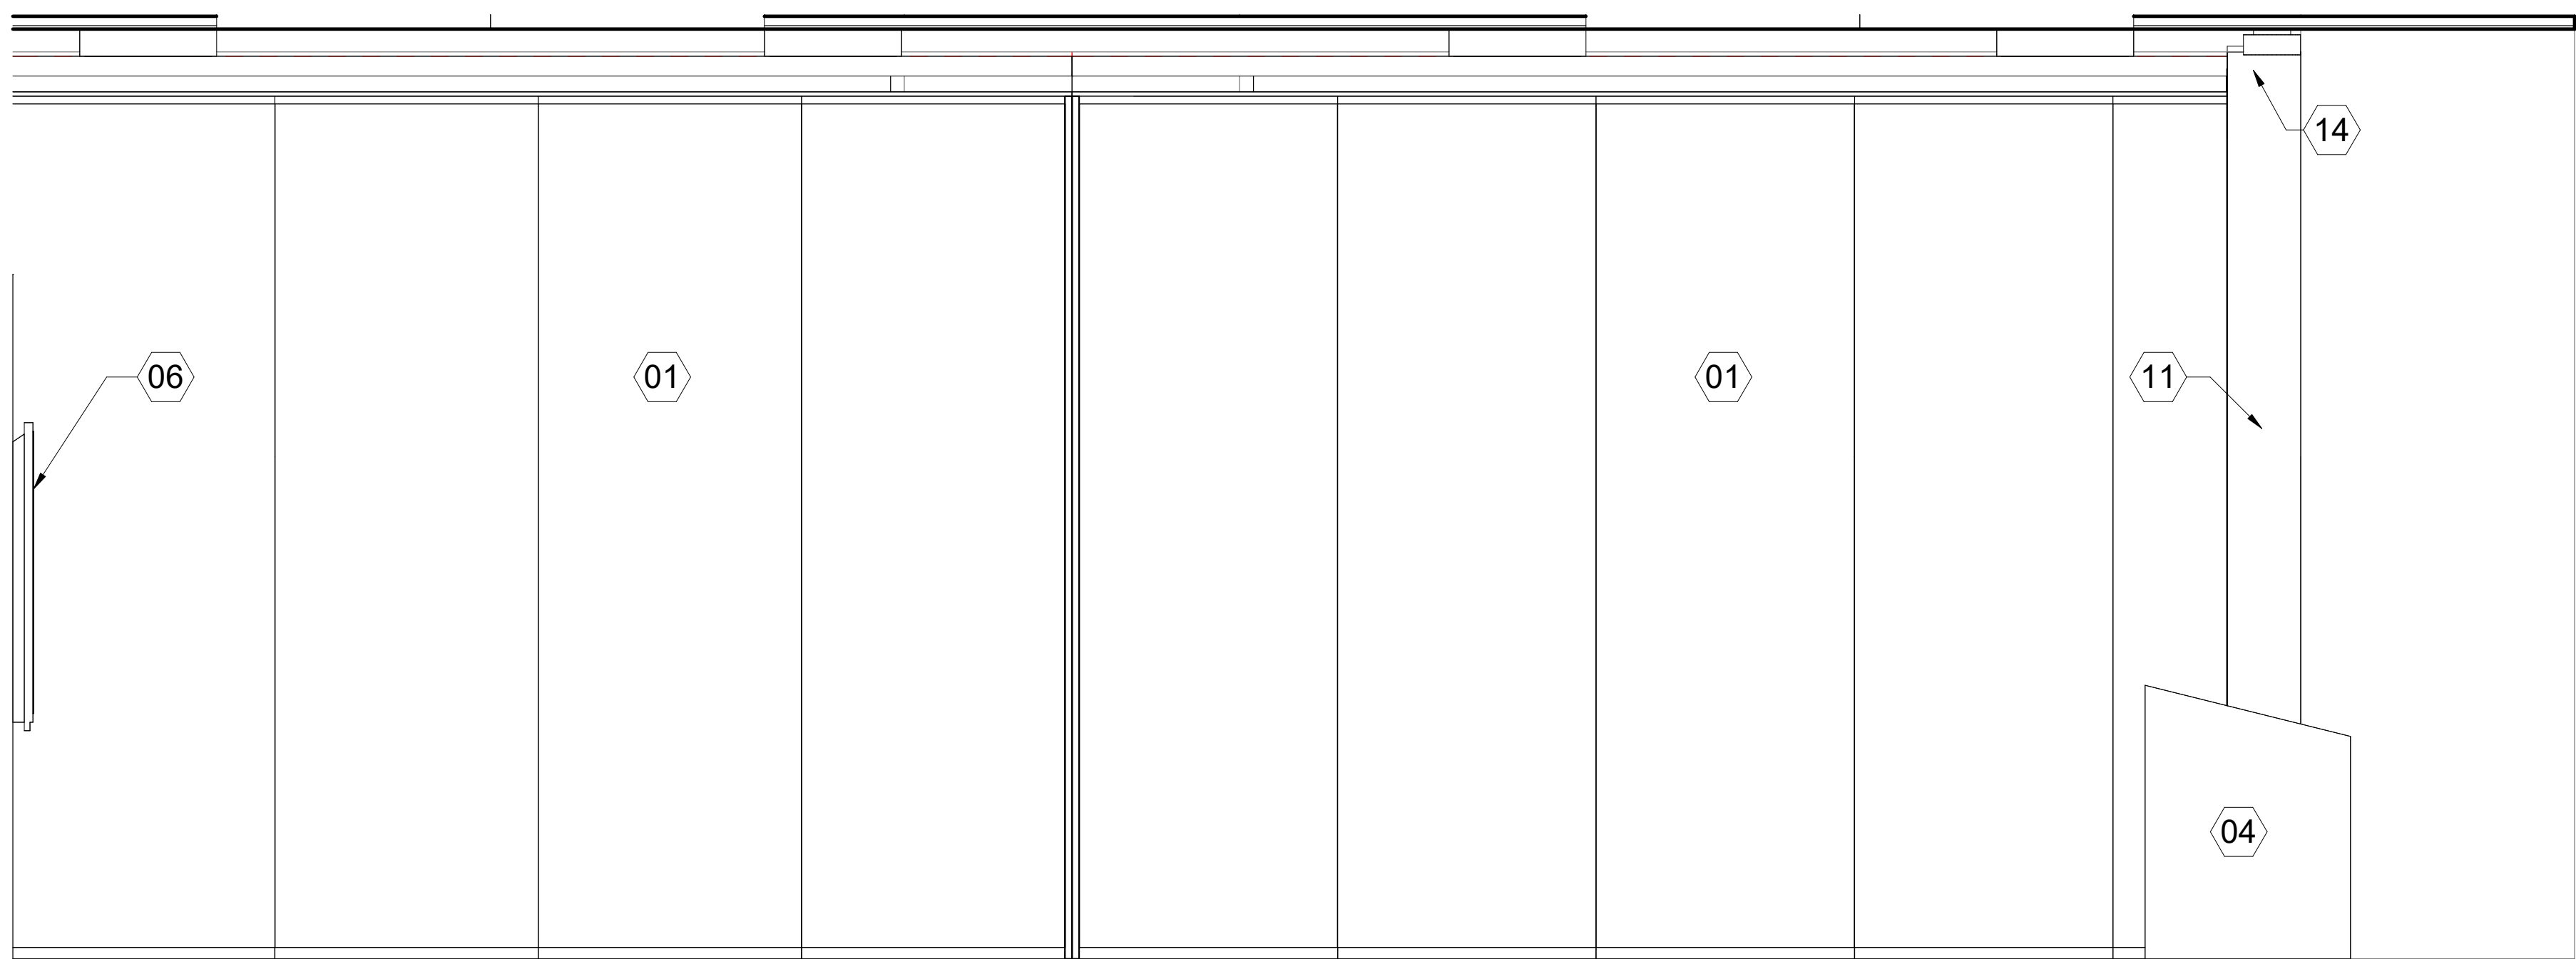

(F1) 1H122-EAST ELEVATION
1/2" = 1'-0"

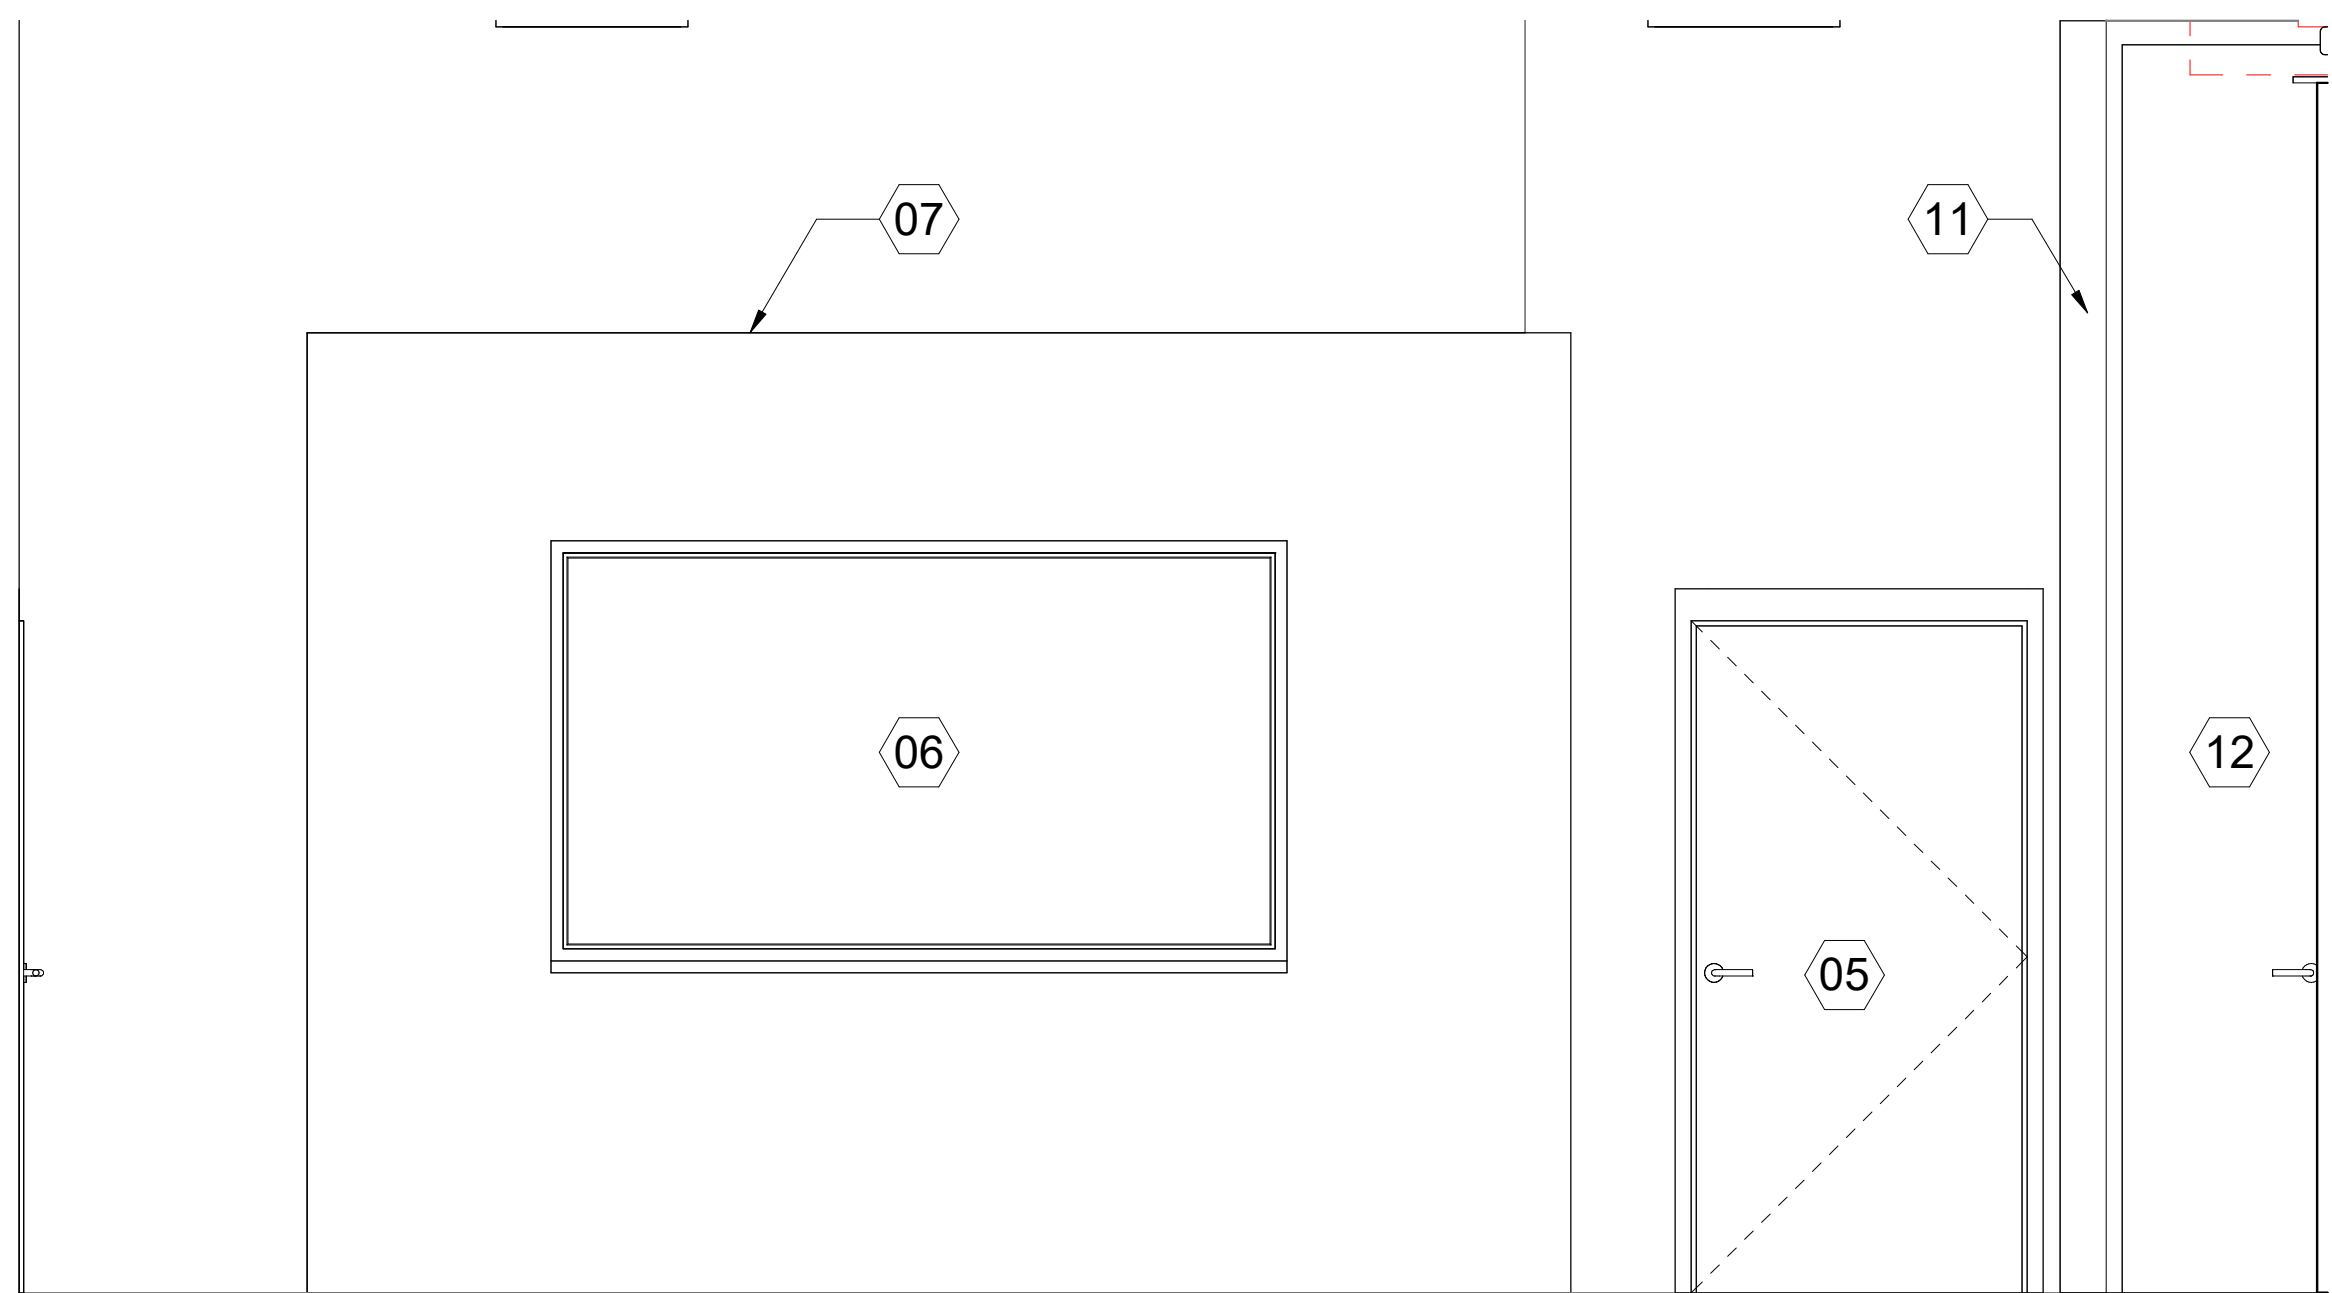

(F6) 1H122-NORTH ELEVATION
1/2" = 1'-0"

[illegible]

CONSULTANT

ARCHITECT/ENGINEER OF RECORD

STAMP

VASNHCS

Project Management and Construction Management Services

VA

U.S. Department
of Veterans Affairs

Drawing Title

NEW WORK ENLARGED INTERIOR VIEWS

Approved: Project Manager/COR
Department of Veteran Affairs, NCA
POC:
Phone:
Email:

Phase

DESIGN SUPPORT

Project Title

ASSIGNMENT No. 49: DESIGN SUPPORT FOR RENOVATE EDUCATION BLDG TRAINING HUB

Location
Las Vegas, NV

Issue Date	03/13/2026
------------	------------

Checked
Checke

Drawn

Author


Project Number


593-26-302

Building Number	001
-----------------	-----

Drawing Number

A-402

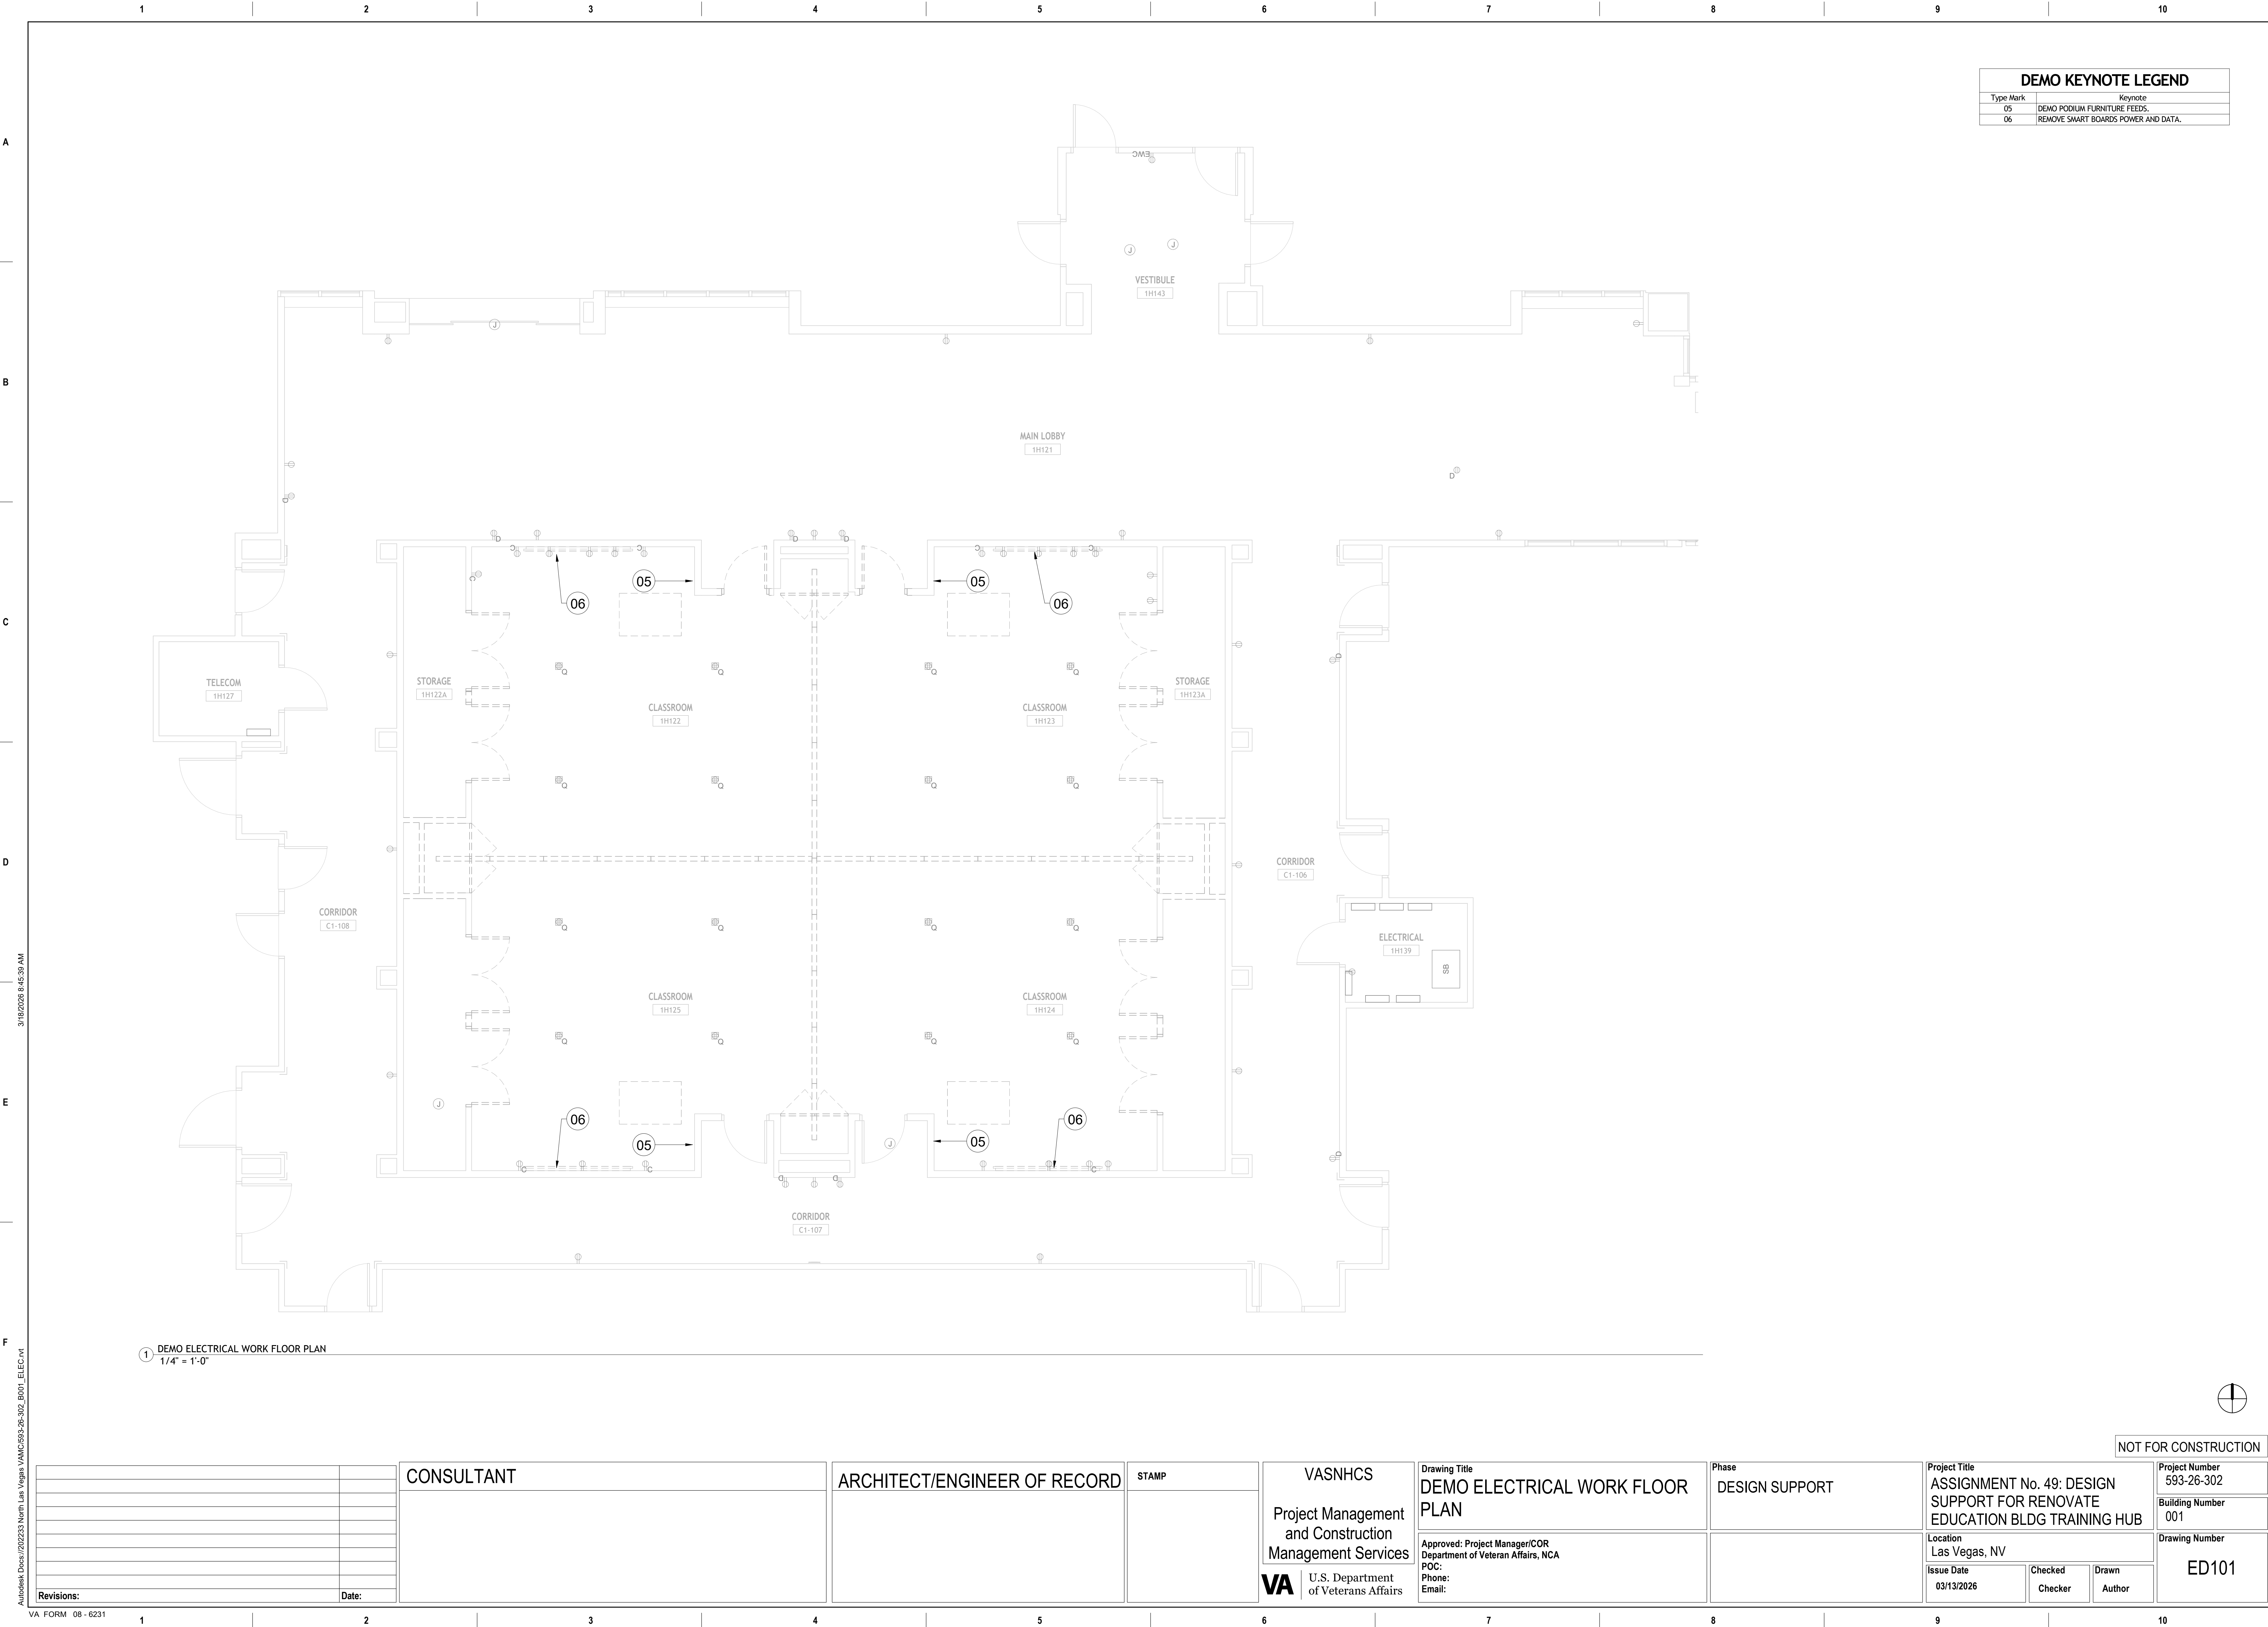

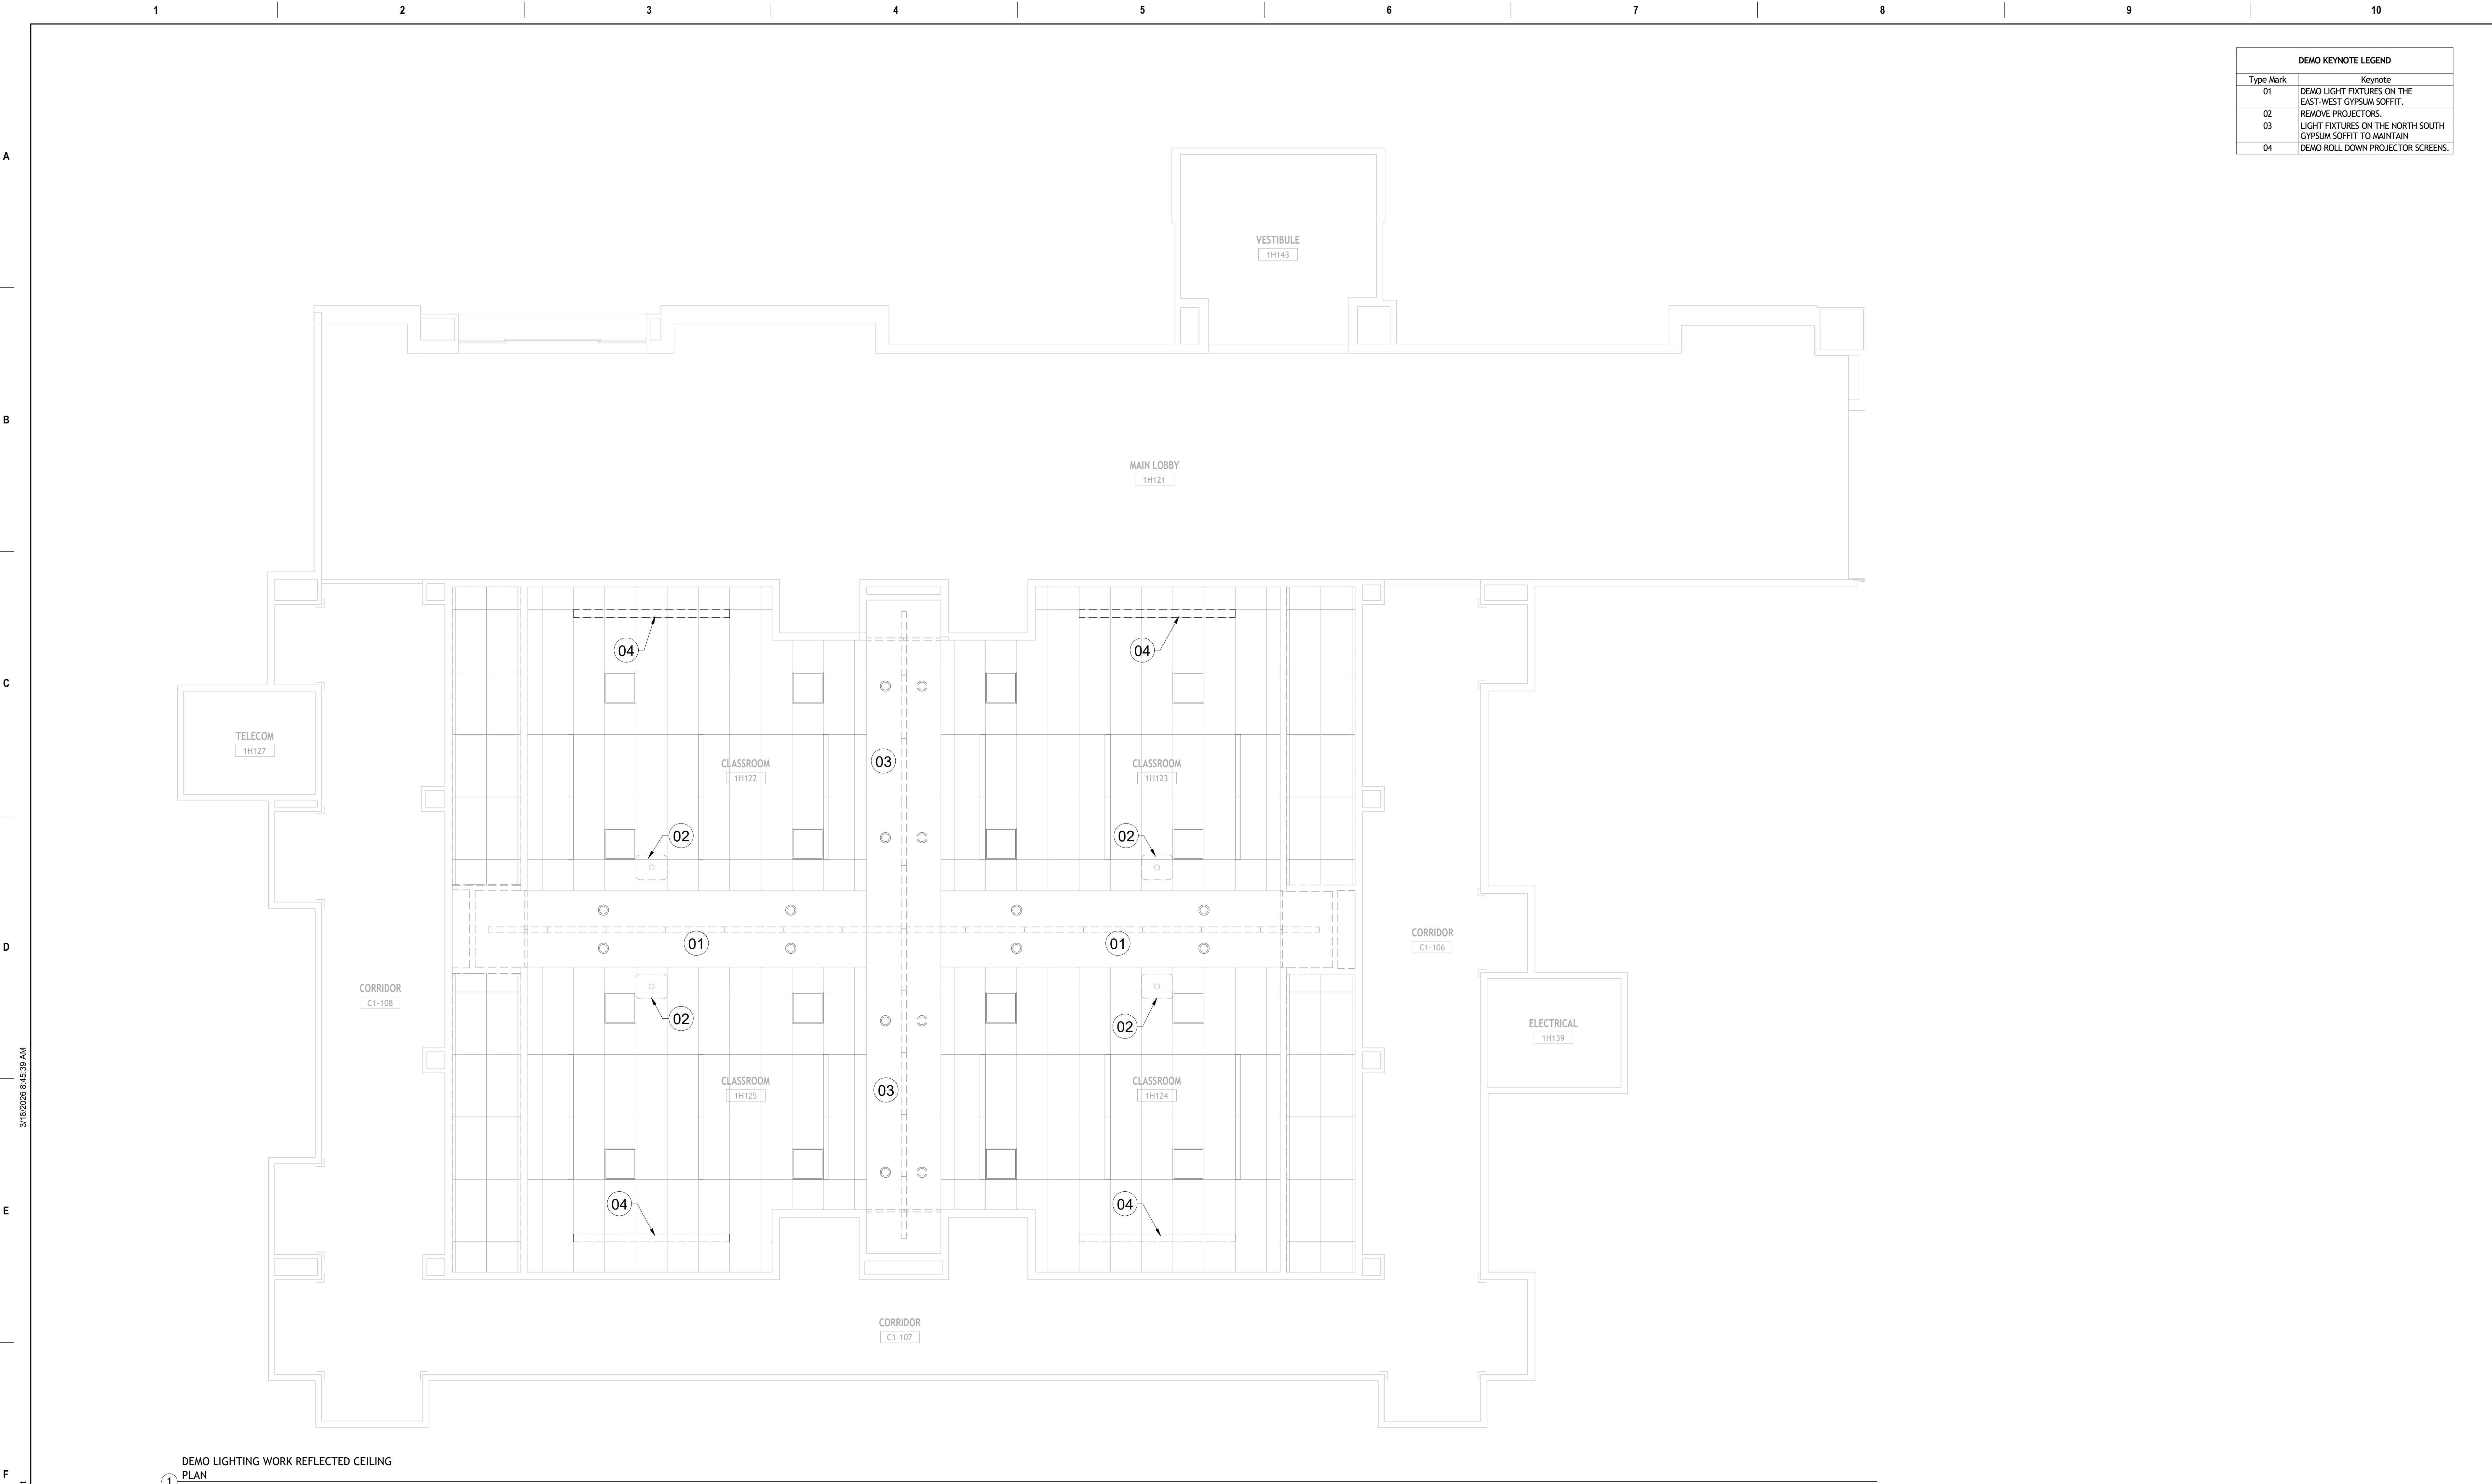


DEMO KEYNOTE LEGEND	
Type Mark	Keynote
01	DEMO LIGHT FIXTURES ON THE EAST-WEST GYPSUM SOFFIT. REMOVE PROJECTORS.
02	REMOVE PROJECTORS.
03	LIGHT FIXTURES ON THE NORTH-SOUTH GYPSUM SOFFIT TO MAINTAIN
04	DEMO ROLL DOWN PROJECTOR SCREENS.

DEMO LIGHTING WORK REFLECTED CEILING
PLAN
1/4" = 1'-0"

NOT FOR CONSTRUCTION

Revisions:	Date:	CONSULTANT	ARCHITECT/ENGINEER OF RECORD	STAMP	VASNHCS Project Management and Construction Management Services VA U.S. Department of Veterans Affairs	Drawing Title DEMO LIGHTING WORK REFLECTED CEILING PLAN Approved: Project Manager/COR Department of Veteran Affairs, NCA POC: Phone: Email:	Phase DESIGN SUPPORT	Project Title ASSIGNMENT No. 49: DESIGN SUPPORT FOR RENOVATE EDUCATION BLDG TRAINING HUB Location Las Vegas, NV Issue Date 03/13/2026	Project Number 593-26-302 Building Number 001 Drawing Number ED102
								Checked Checker	Drawn Author

3/16/2026 8:45:39 AM
AutoCAD Doc: 202223 North Las Vegas VAMC/593-26-302_B001_ELEC.rvt
VA FORM 08 - 6231

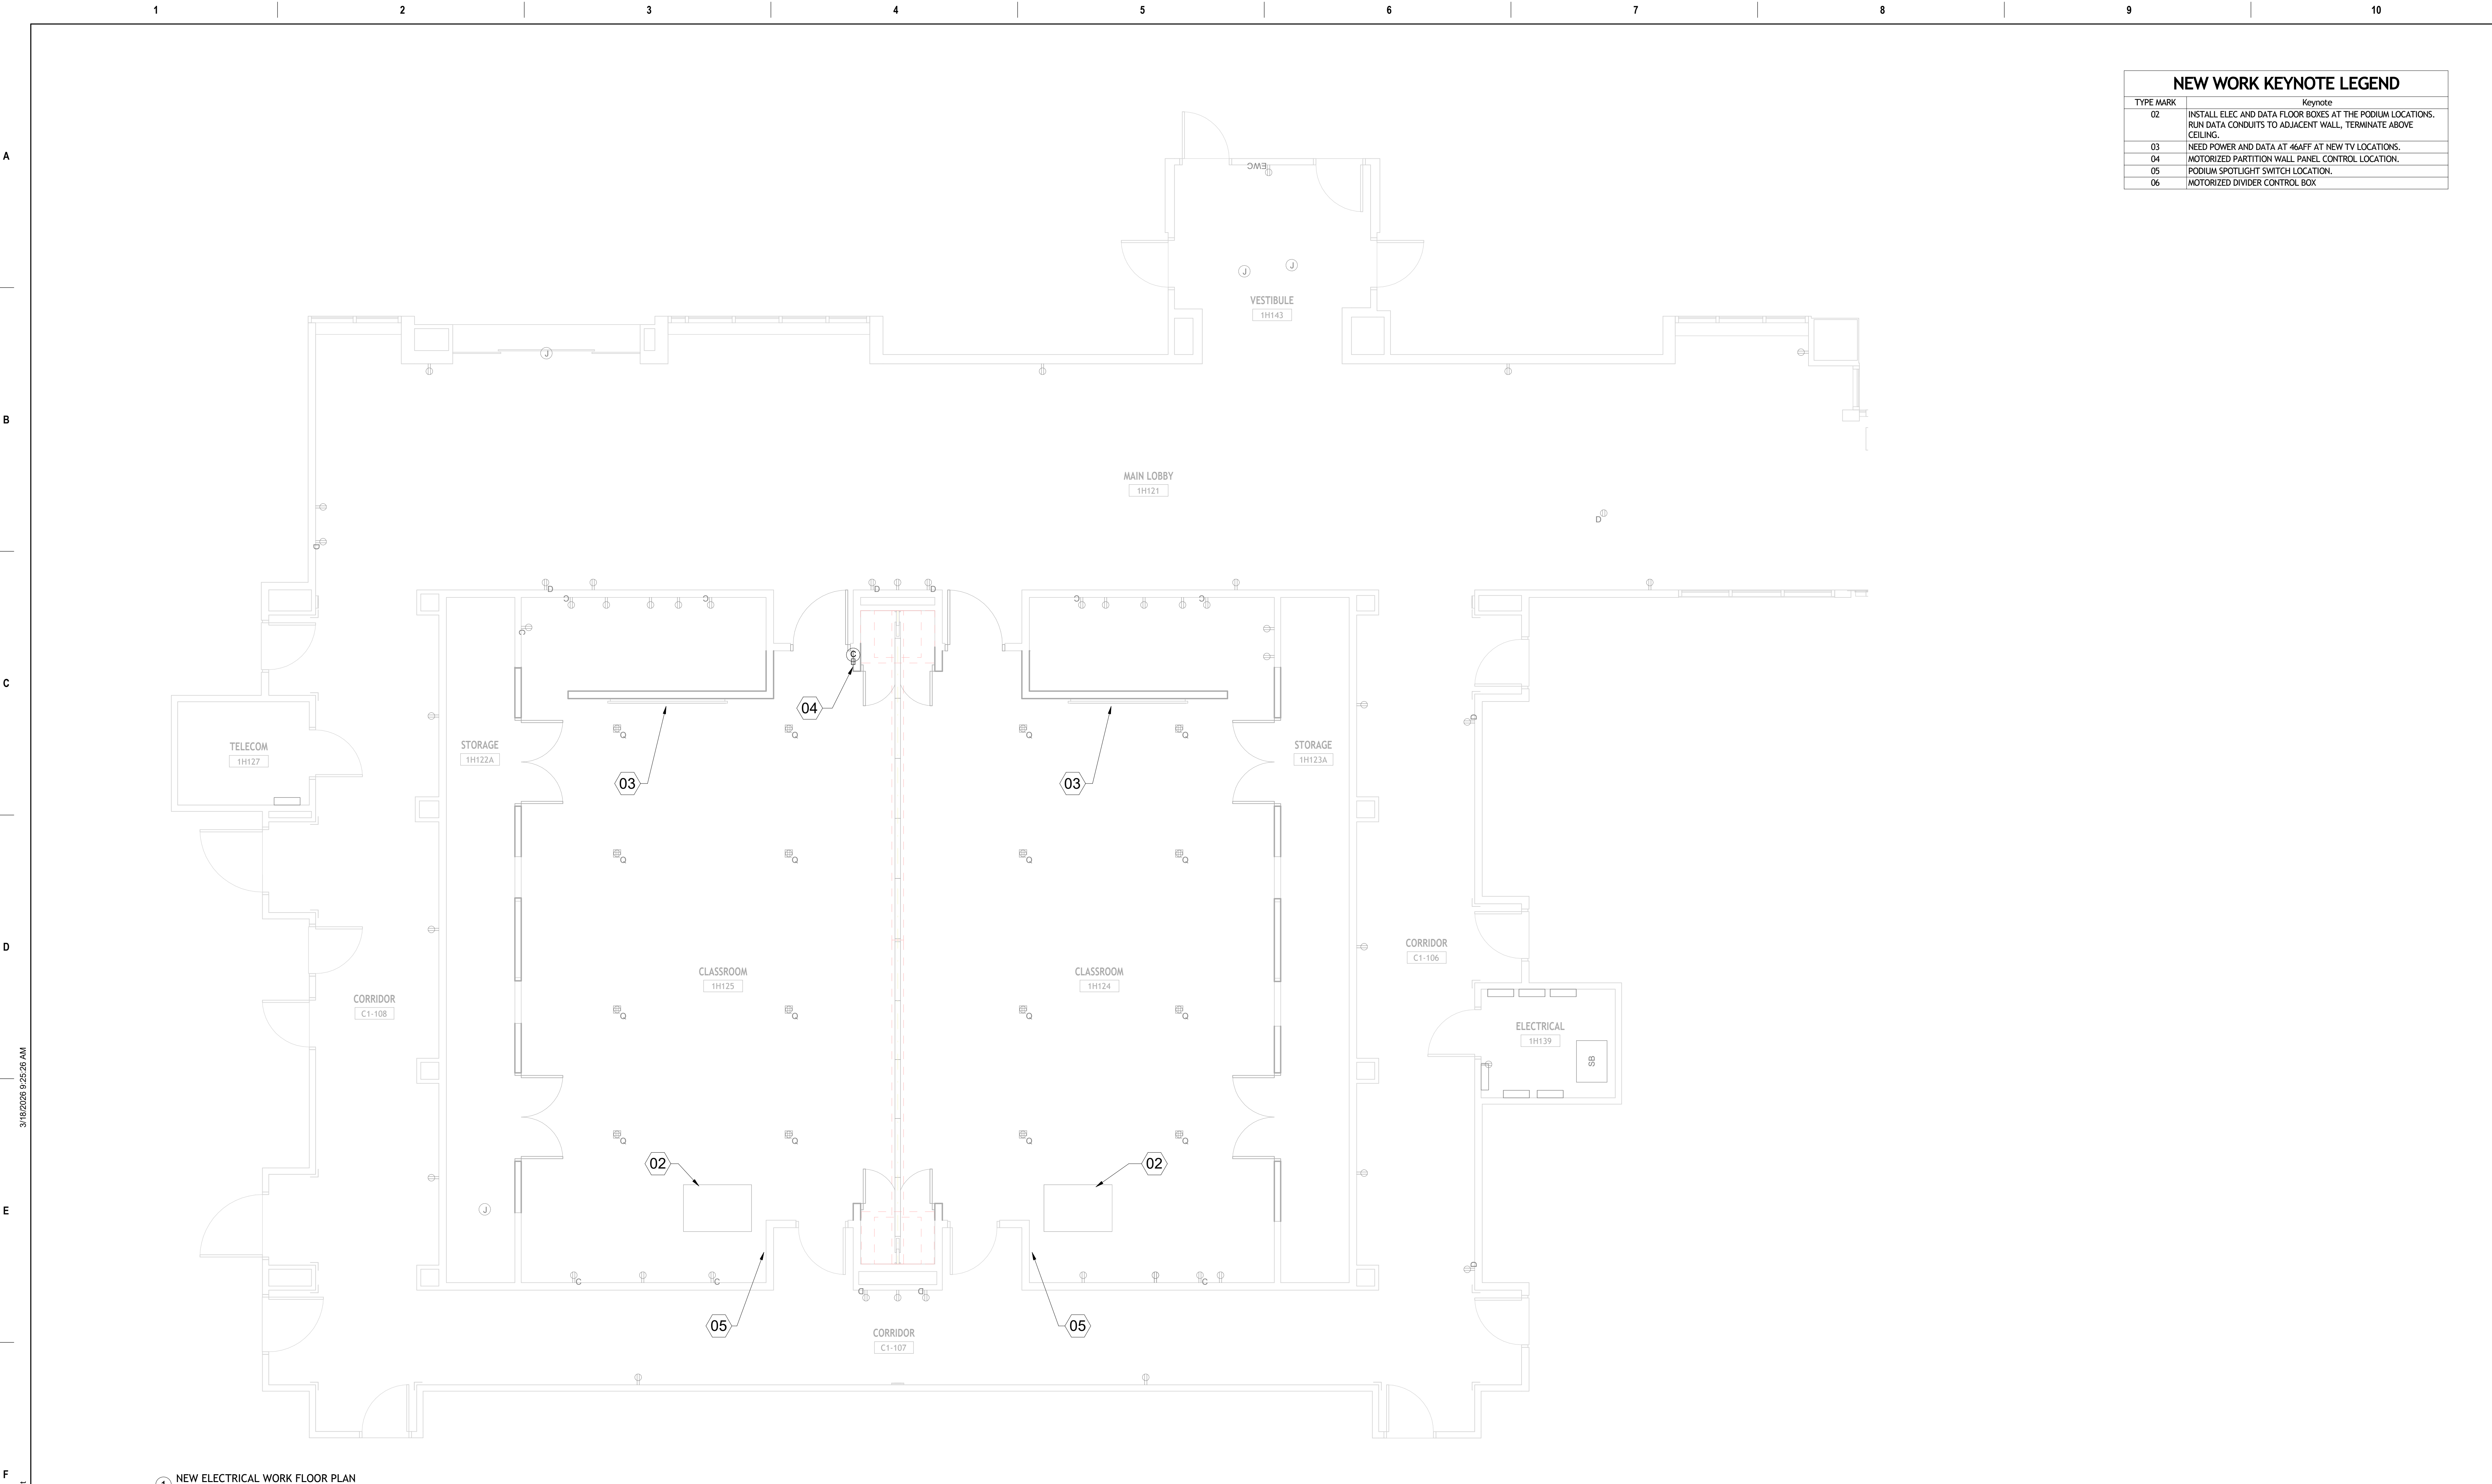

NEW WORK KEYNOTE LEGEND	
TYPE MARK	Keynote
02	INSTALL ELEC. AND DATA FLOOR BOXES AT THE PODIUM LOCATIONS. RUN DATA CONDUITS TO ADJACENT WALL, TERMINATE ABOVE CEILING.
03	NEED POWER AND DATA AT 46AFF AT NEW TV LOCATIONS.
04	MOTORIZED PARTITION WALL PANEL CONTROL LOCATION.
05	PODIUM SPOTLIGHT SWITCH LOCATION.
06	MOTORIZED DIVIDER CONTROL BOX

1 NEW ELECTRICAL WORK FLOOR PLAN
1/4" = 1'-0"

NOT FOR CONSTRUCTION

Revisions:	Date:

CONSULTANT

ARCHITECT/ENGINEER OF RECORD

STAMP

VASNHCS Project Management and Construction Management Services VA U.S. Department of Veterans Affairs


Drawing Title NEW ELECTRICAL WORK FLOOR PLAN Approved: Project Manager/COR Department of Veteran Affairs, NCA POC: Phone: Email:

Phase DESIGN SUPPORT

Project Title ASSIGNMENT No. 49: DESIGN SUPPORT FOR RENOVATE EDUCATION BLDG TRAINING HUB
Location Las Vegas, NV
Issue Date 03/13/2026
Checked Checker
Drawn Author

Project Number 593-26-302
Building Number 001
Drawing Number E-101

3/18/2026 9:25:28 AM
Autodesk Docs/202223 North Las Vegas VAMC/593-26-302_B001_ELEC.rvt
VA FORM 08 - 6231

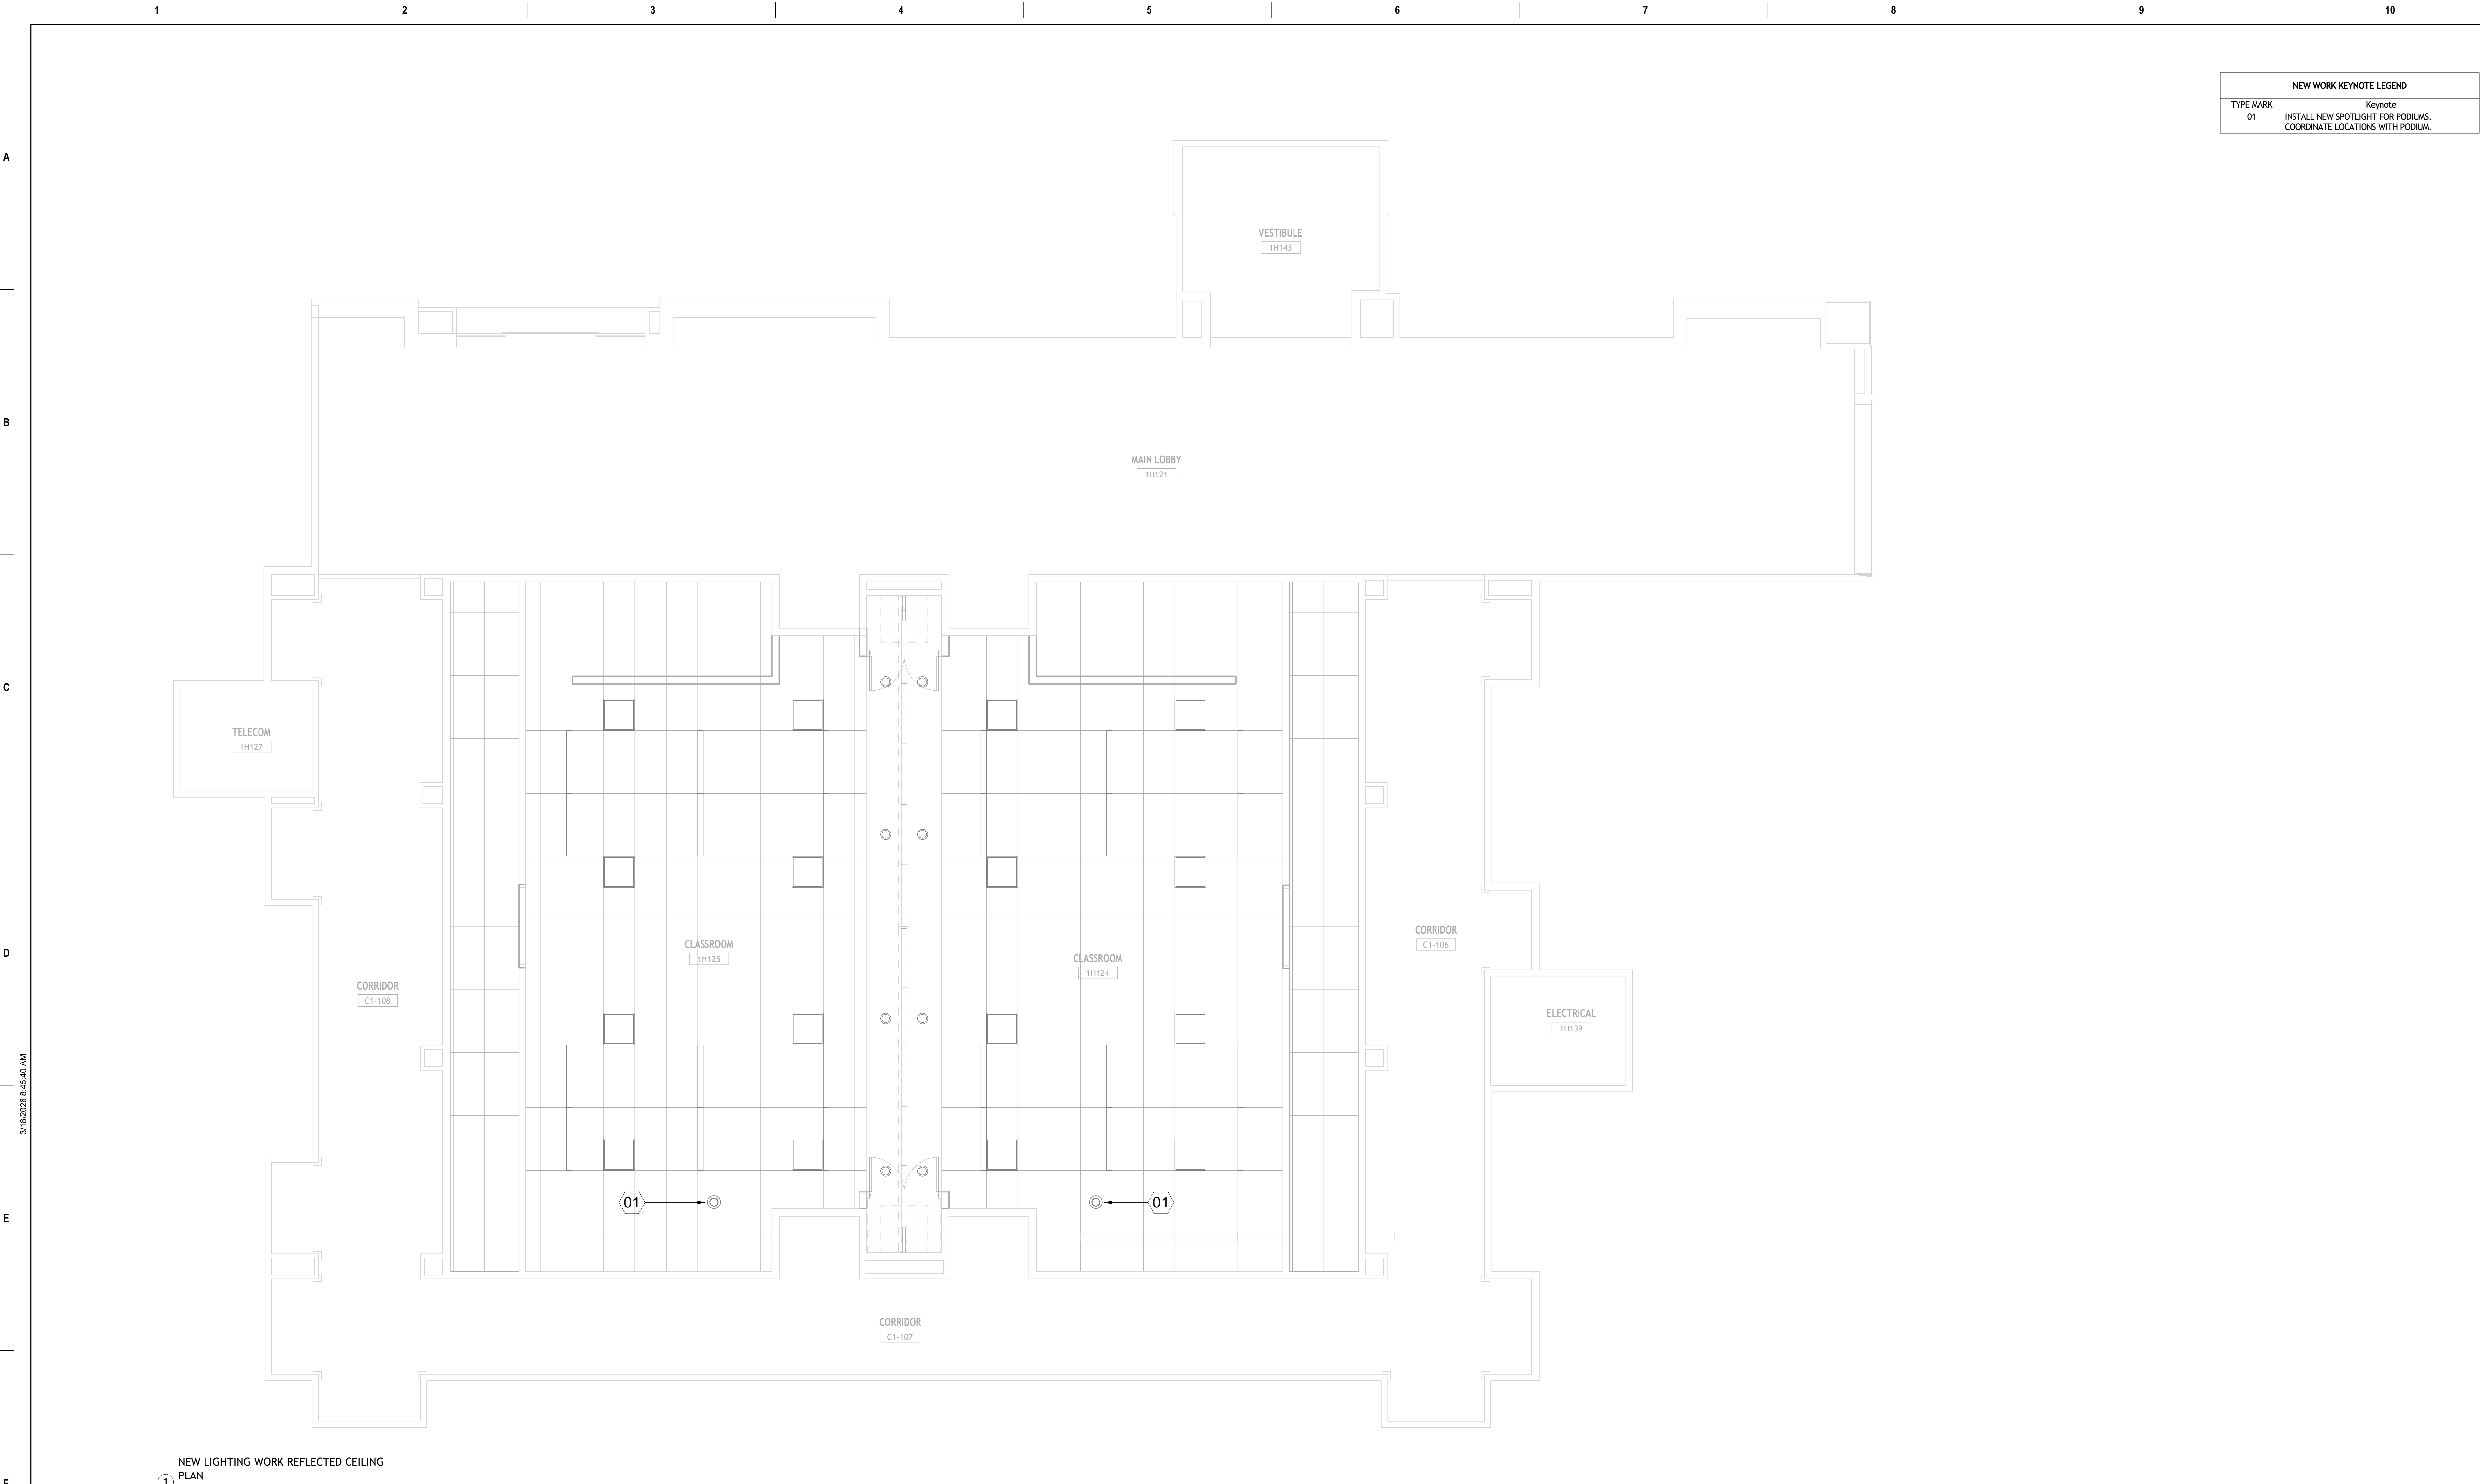

NEW WORK KEYNOTE LEGEND		
TYPE MARK	Keynote	
01	INSTALL NEW SPOTLIGHT FOR PODIUMS, COORDINATE LOCATIONS WITH PODIUM.	

NEW LIGHTING WORK REFLECTED CEILING
PLAN
1/4" = 1'-0"

NOT FOR CONSTRUCTION

		CONSULTANT		ARCHITECT/ENGINEER OF RECORD	STAMP	VASNHCS Project Management and Construction Management Services VA U.S. Department of Veterans Affairs	Drawing Title	Phase	Project Title	Project Number
							NEW LIGHTING WORK REFLECTED	DESIGN SUPPORT	ASSIGNMENT No. 49: DESIGN	593-26-302
							CEILING PLAN		SUPPORT FOR RENOVATE	Building Number
									EDUCATION BLDG TRAINING HUB	001
										Drawing Number
							Approved: Project Manager/COR Department of Veteran Affairs, NCA		Location	
							POC:		Las Vegas, NV	
							Phone:		Issue Date	Checked
							Email:		03/13/2026	Checker
										Drawn
										Author
Revisions:		Date:								E-102

3/18/2026 8:45:40 AM
Autodesk Docs: 202223 North Las Vegas VAMC/593-26-302_B001_ELEC.rvt
VA FORM 08 - 6231