


GENERAL NOTES

1. PROTECT ALL EXISTING WORK FROM DAMAGE DURING CONSTRUCTION. ANY DAMAGED MATERIALS, SYSTEMS, COMPONENTS, FINISHES AND THE LIKE, SHALL BE REPAIRED OR REPLACED AT THE EXPENSE OF THE CONTRACTOR TO THE ACCEPTANCE OF THE OWNER.
2. SEAL ALL INTERIOR WALL AND CEILING PENETRATIONS TO MATCH EXISTING FIRE RATING OR NEW FIRE RATING, IF REQUIRED. COORDINATE WITH ARCHITECTURAL DRAWINGS AS REQUIRED.
3. ALL TELECOMMUNICATIONS CABLING CATEGORY 6 AND BELOW SHALL BE REMOVED AND REPLACED WITH CAT6A PORTS AND CABLE QUANTITIES INDICATED, UNLESS NOTED OTHERWISE.
4. TELECOMMUNICATIONS CABLES SHALL BE ROUTED IN EXISTING PATHWAY VACATED BY EXISTING CABLING. PROVIDE RACEWAYS TO EXTEND TO ASSOCIATED TR.
5. A TELECOMMUNICATIONS OUTLET UPGRADE SHALL INCLUDE, BUT IS NOT LIMITED TO REMOVING AND DISPOSING EXISTING DEVICES AND CABLES; PROVIDING ALL LABOR, MATERIALS, TOOLS, TEST INSTRUMENTS, AND CONSUMABLES REQUIRED FOR THE INSTALLATION, TERMINATION, TESTING, LABELING, AND CERTIFICATION OF A FULLY FUNCTIONAL CATEGORY 6A OUTLET WITH THE PORT QUANTITY INDICATED.
6. WHERE NEW DATA OUTLETS ARE BEING PROVIDED AND EXISTING DATA OUTLET CURRENTLY DOES NOT EXIST, PROVIDE (1) 1" CONDUIT FROM NEW BACKBOX TO ACCESSIBLE CEILING SPACE TO SECURELY ROUTE DATA CABLING FROM OUTLET TO TR VIA CABLE TRAY. IF CABLE TRAY IS NON-EXISTENT, EXTEND RACEWAY FROM OUTLET TO TR AS REQUIRED.
7. PROVIDE CONDUITS AND SLEEVES AS REQUIRED FOR ROUTING AND INSTALLATION OF HORIZONTAL AND BACKBONE CABLING. PROVIDE FIRE-STOP MATERIALS TO SEAL IN AND AROUND CONDUIT PER CODE. REFER TO ARCHITECTURAL DRAWINGS FOR PARTITION TYPES AND WALL HEIGHTS.
8. ALL TELECOMMUNICATION ROOMS SHALL BE PROVIDED WITH FIRE-RATED PLYWOOD BACKBOARDS. REFERENCE EXACT PLACEMENTS WITH ARCHITECTURE DRAWINGS AS REQUIRED.
9. ANY LIVE SYSTEMS IN DEMO'D TR'S MUST REMAIN LIVE. CONTRACTOR TO COORDINATE WITH THE STATION TO IDENTIFY SYSTEMS THAT ARE LIVE. IF SYSTEMS ARE LIVE; INSTALL NEW CABLE FROM DEMO'D TR TO NEW TR. REFER TO DETAIL '3' ON TN506.


KEY NOTES

1. EXISTING DATA RACK TO BE DECOMMISSIONED BY VA. CONTRACTOR SHALL COORDINATE WITH VA AS REQUIRED.
2. EXISTING VERTICAL CABLING SLEEVES TO BE PRESERVED. EXISTING FIBER OPTIC AND/OR EXISTING VERTICAL CABLING RELATED TO EXISTING TR RACKS TO BE DEMOLISHED.
3. EXISTING PENETRATIONS WITH CABLING TO BE REMOVED. CONTRACTOR SHALL PATCH AND FIREPROOF OPENINGS. COORDINATE WITH ARCHITECTURAL DRAWINGS AND SPECIFICATIONS.



KEY PLAN

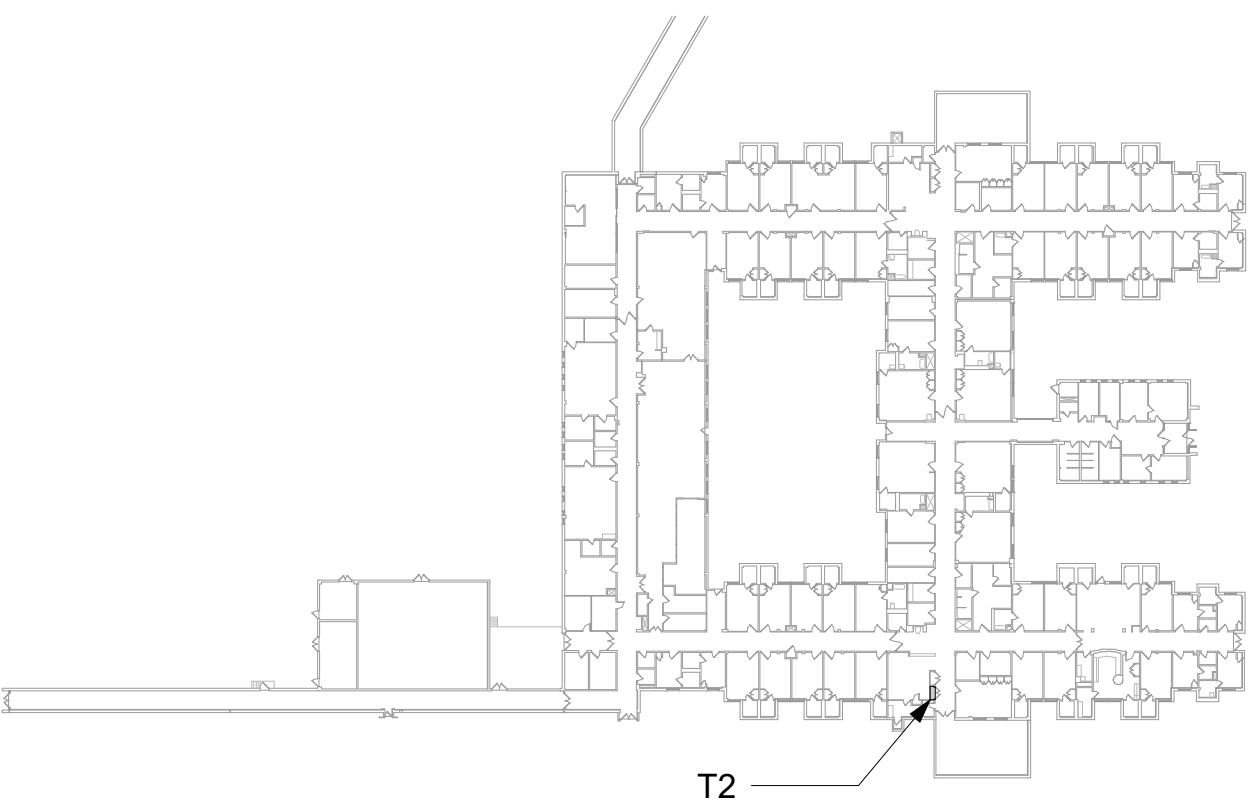



AREA SHOWN

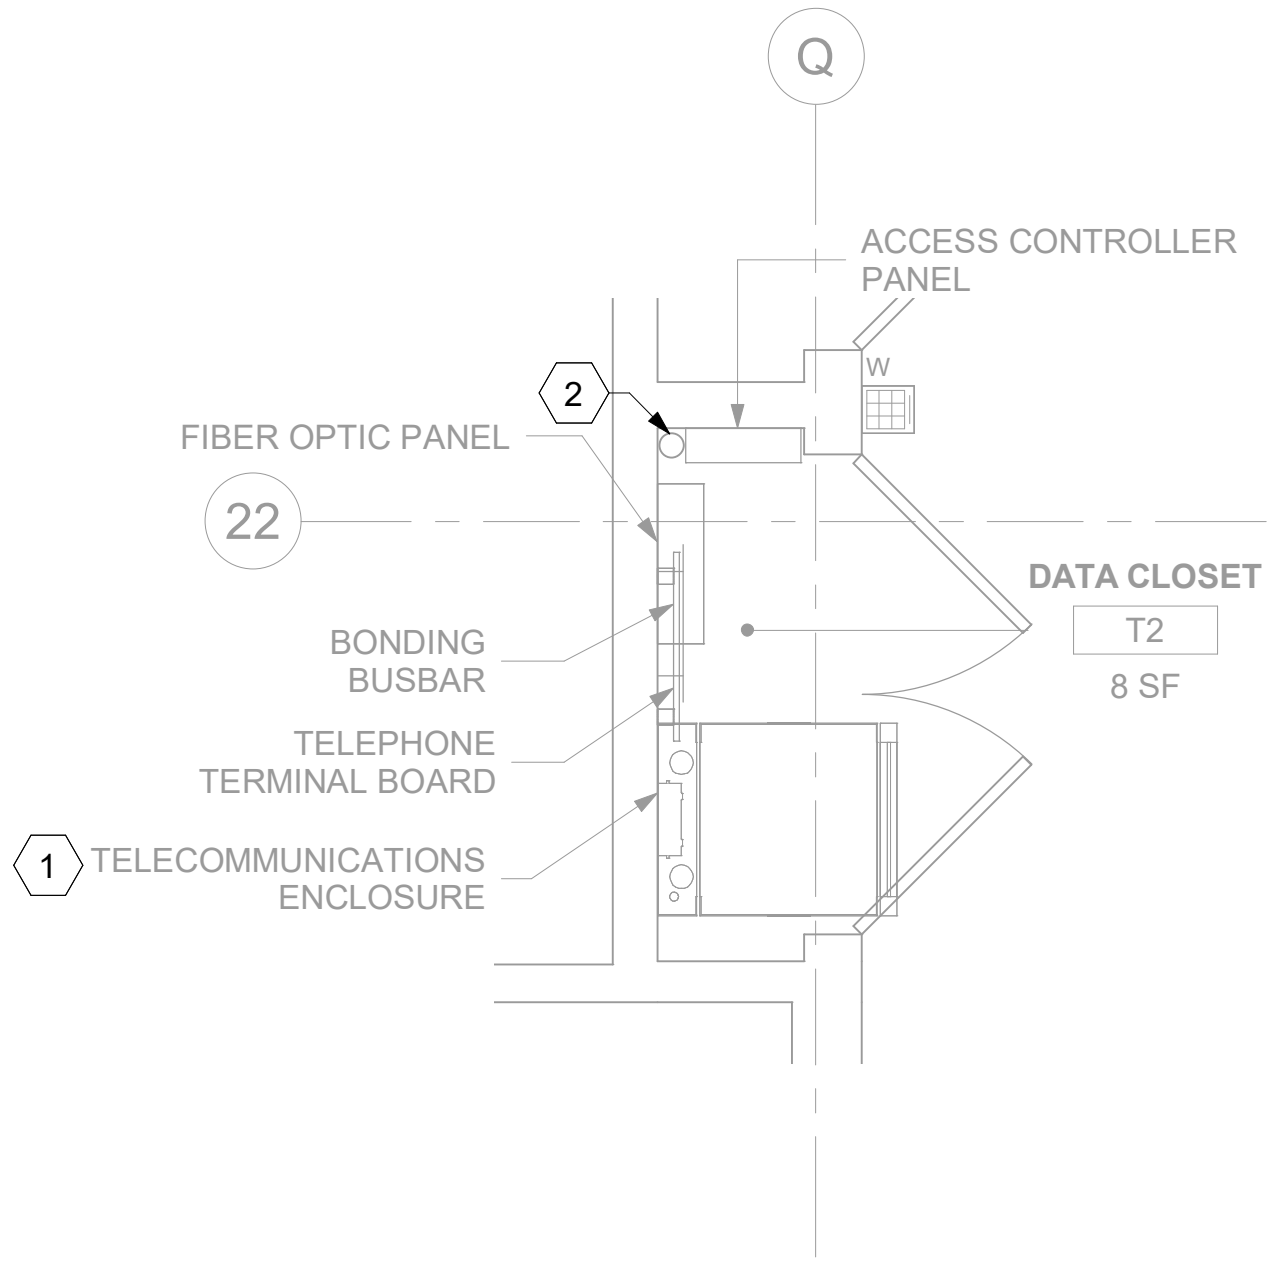



1 RM T2 - DEMOLITION FLOOR PLAN
146TN101A 1/2" = 1'-0"

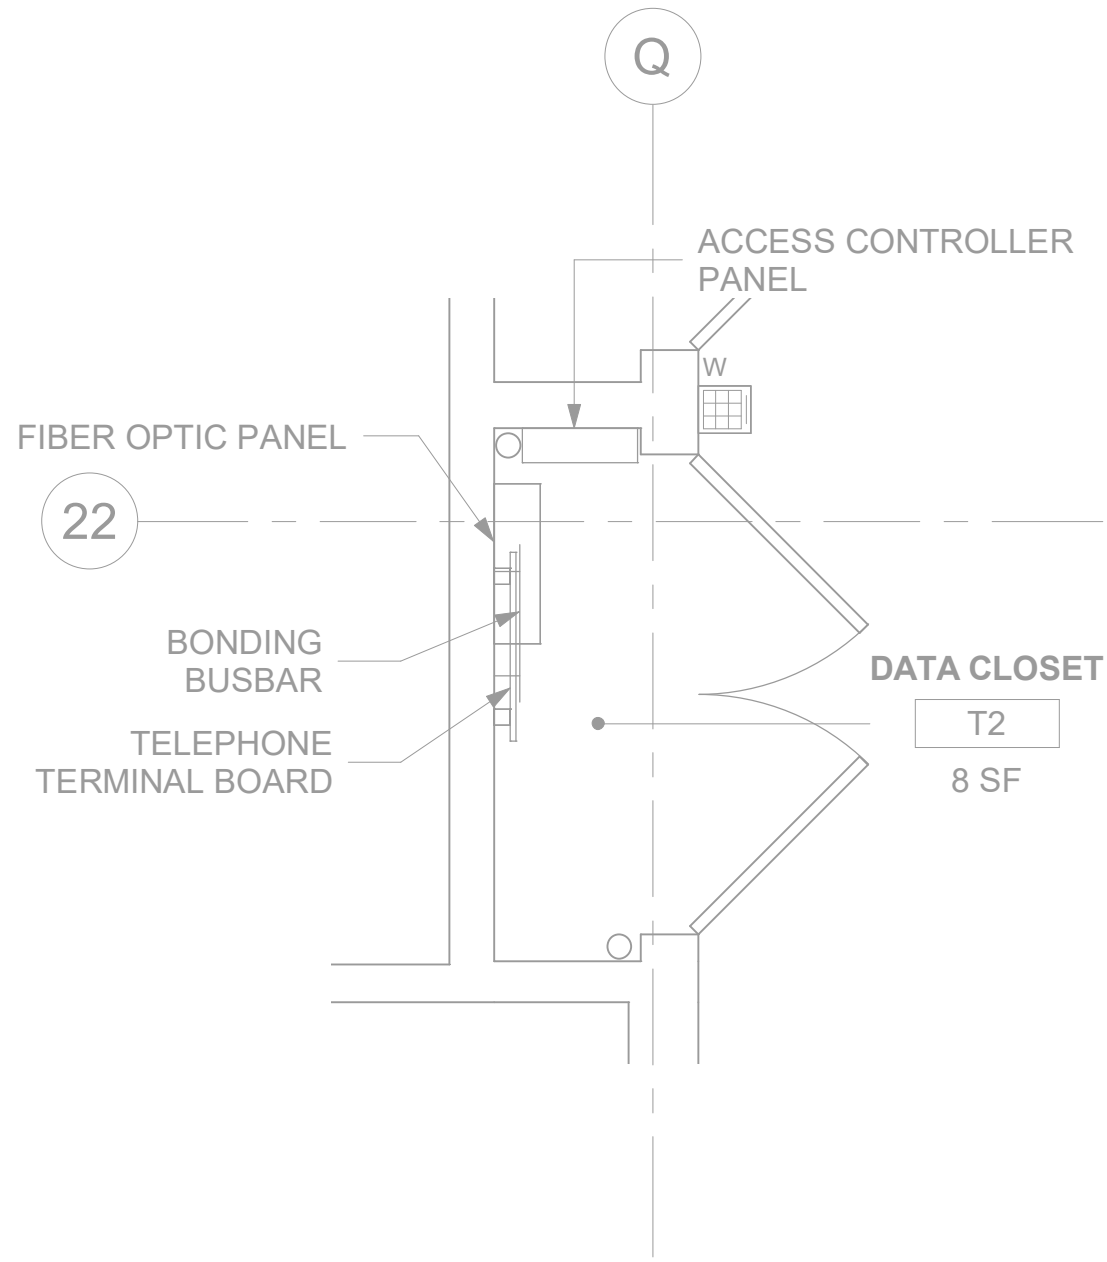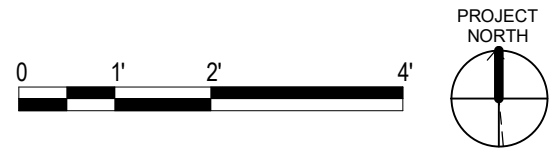


2 RM T2 - TELECOMMUNICATIONS PLAN
146TN101A 1/2" = 1'-0"

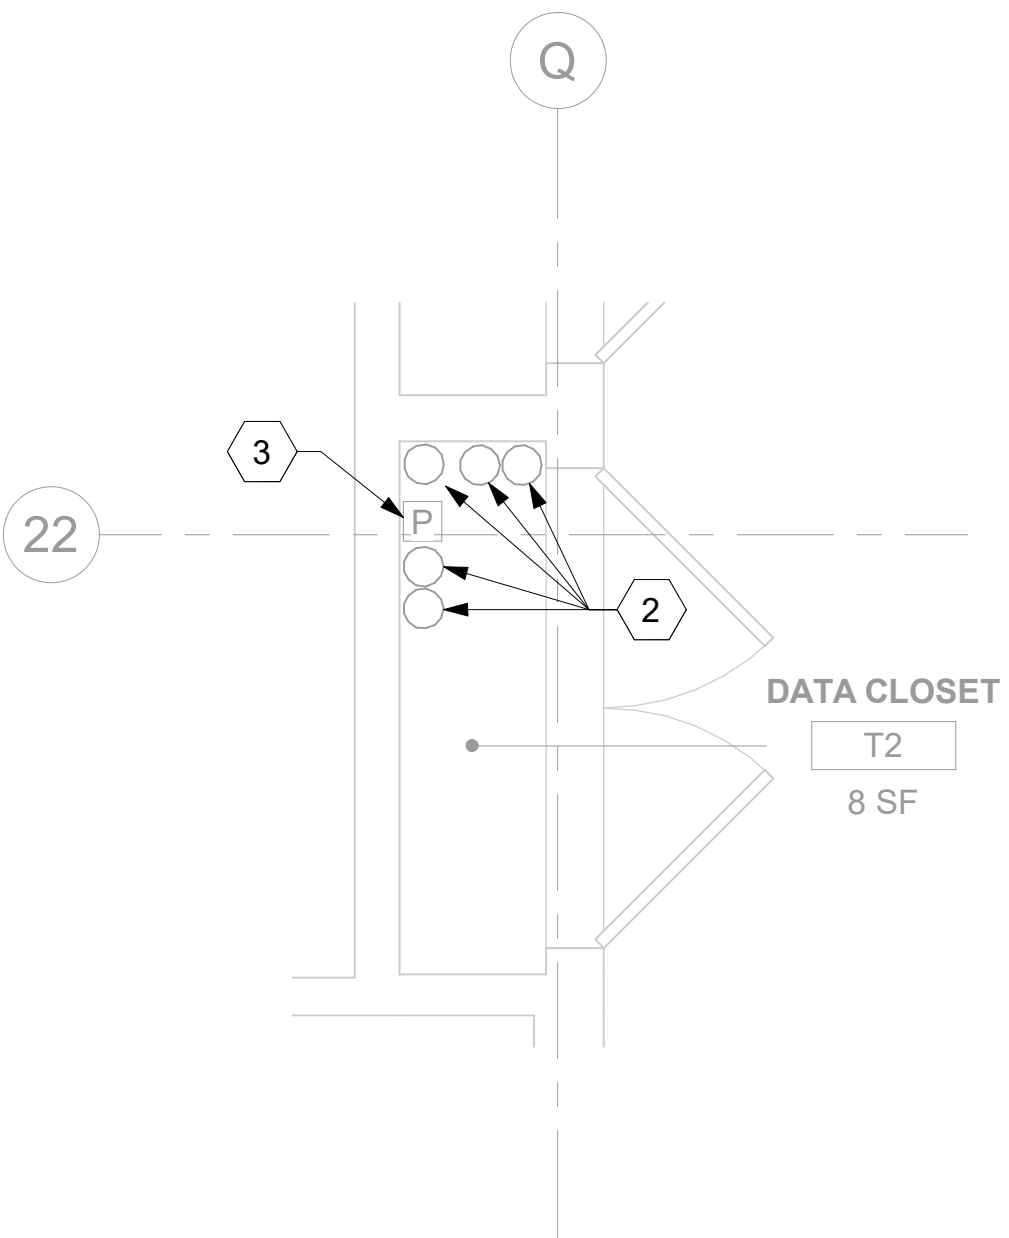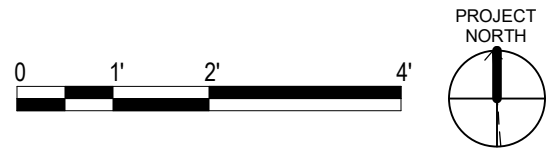



3 RM T2 - DEMOLITION OVERHEAD PLAN
146TN101A 1/2" = 1'-0"

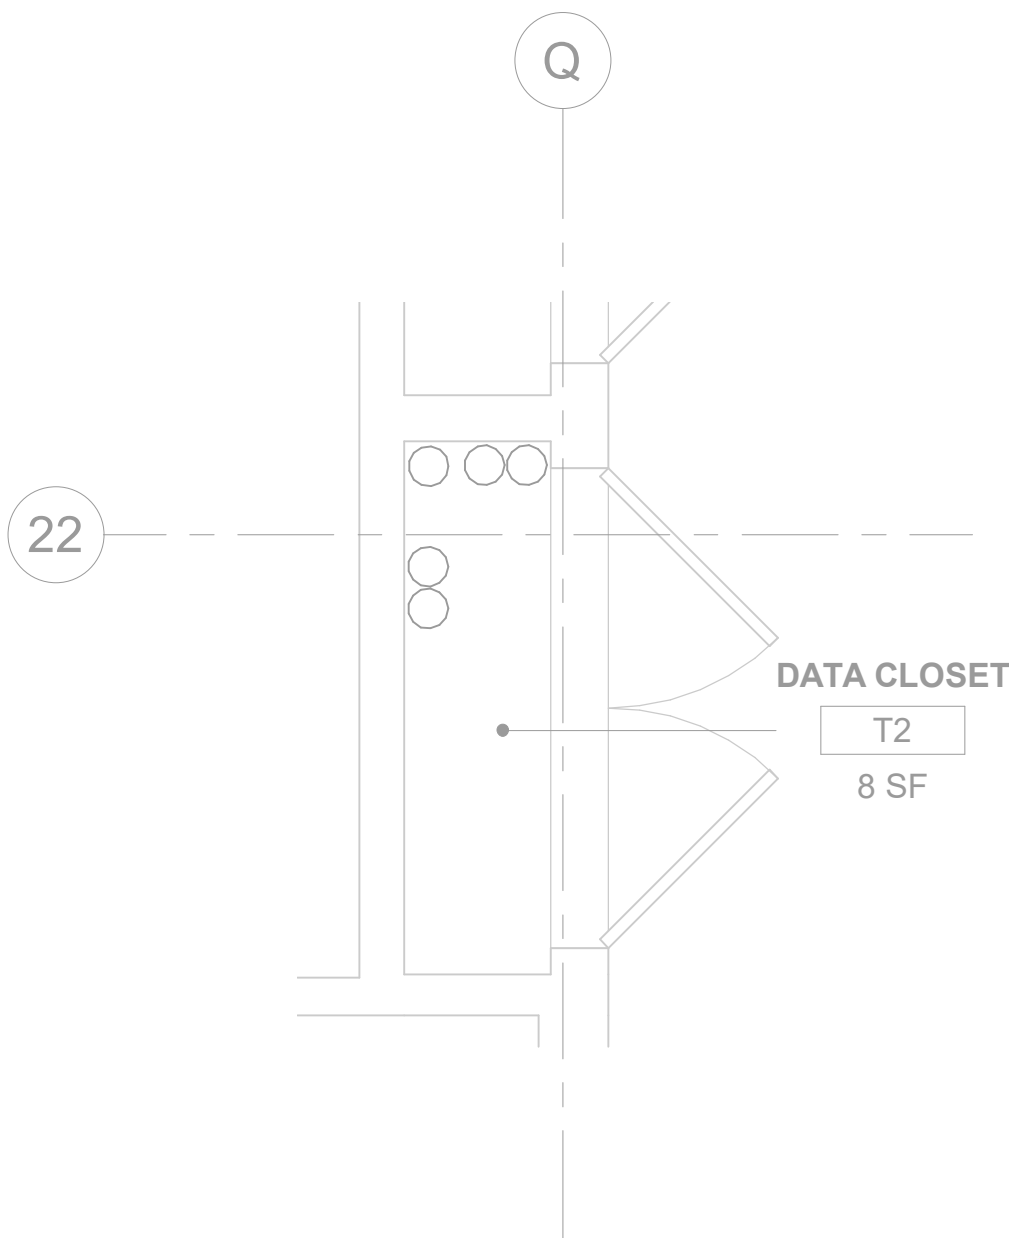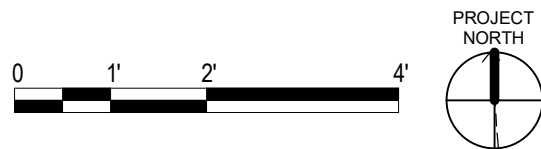


4 RM T2 - OVERHEAD PLAN
146TN101A 1/2" = 1'-0"

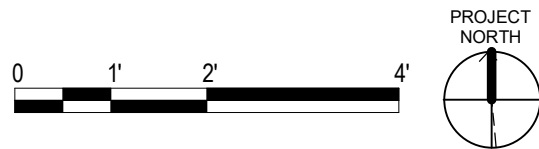

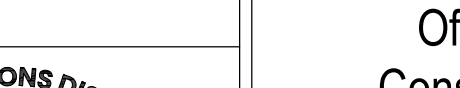
		CONSULTANT	ARCHITECT/ENGINEER OF RECORD	STAMP	Office of Construction and Facilities Management VA U.S. Department of Veterans Affairs	Drawing Title BLDG 146 - LEVEL 01 - ENLARGED TELECOMMUNICATIONS PLANS	Phase 100% CONSTRUCTION DOCUMENTS	Project Title EHRM INFRASTRUCTURE UPGRADES - HAMPTON	Project Number 590-22-700			
		ENGINEERING DISCIPLINE:	A/E: SPEES DESIGN BUILD 23830 PACIFIC HIGHWAY S. SUITE 203 KENT, WA 98032 SPEESDESIGNBUILD			Approved:	FULLY SPRINKLERED	Location HAMPTON VA MEDICAL CENTER, HAMPTON, VIRGINIA	Building Number 146			
Revisions:		Date:						Issue Date 07/18/2025	Checked KG	Drawn BCL/GPB	Drawing Number 146TN401d	
											601 of 713	

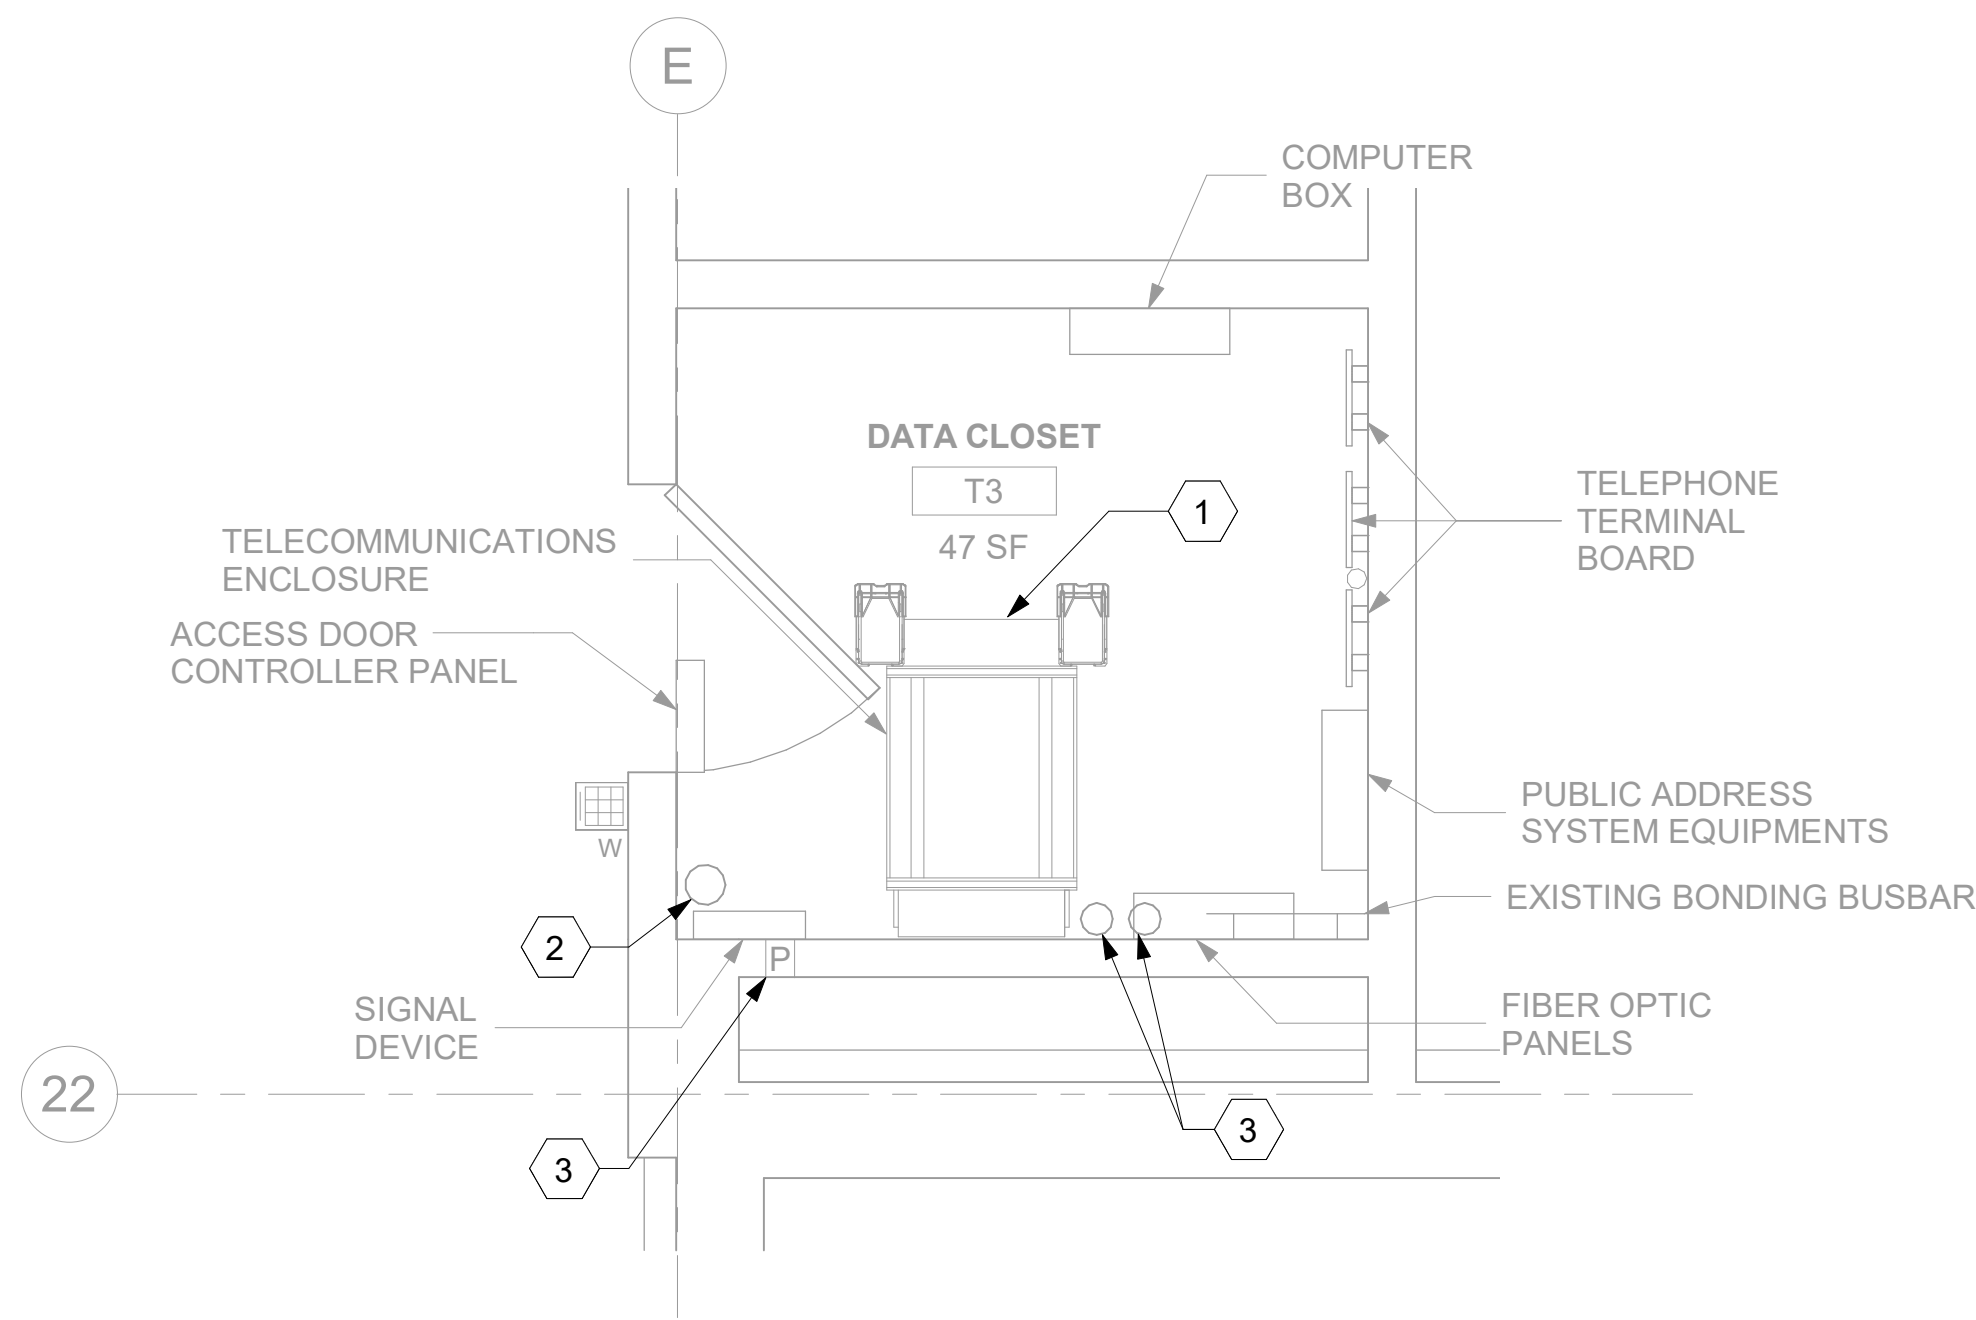


1 RM T3 - DEMOLITION FLOOR PLAN
146TN101A 1/2" = 1'-0"

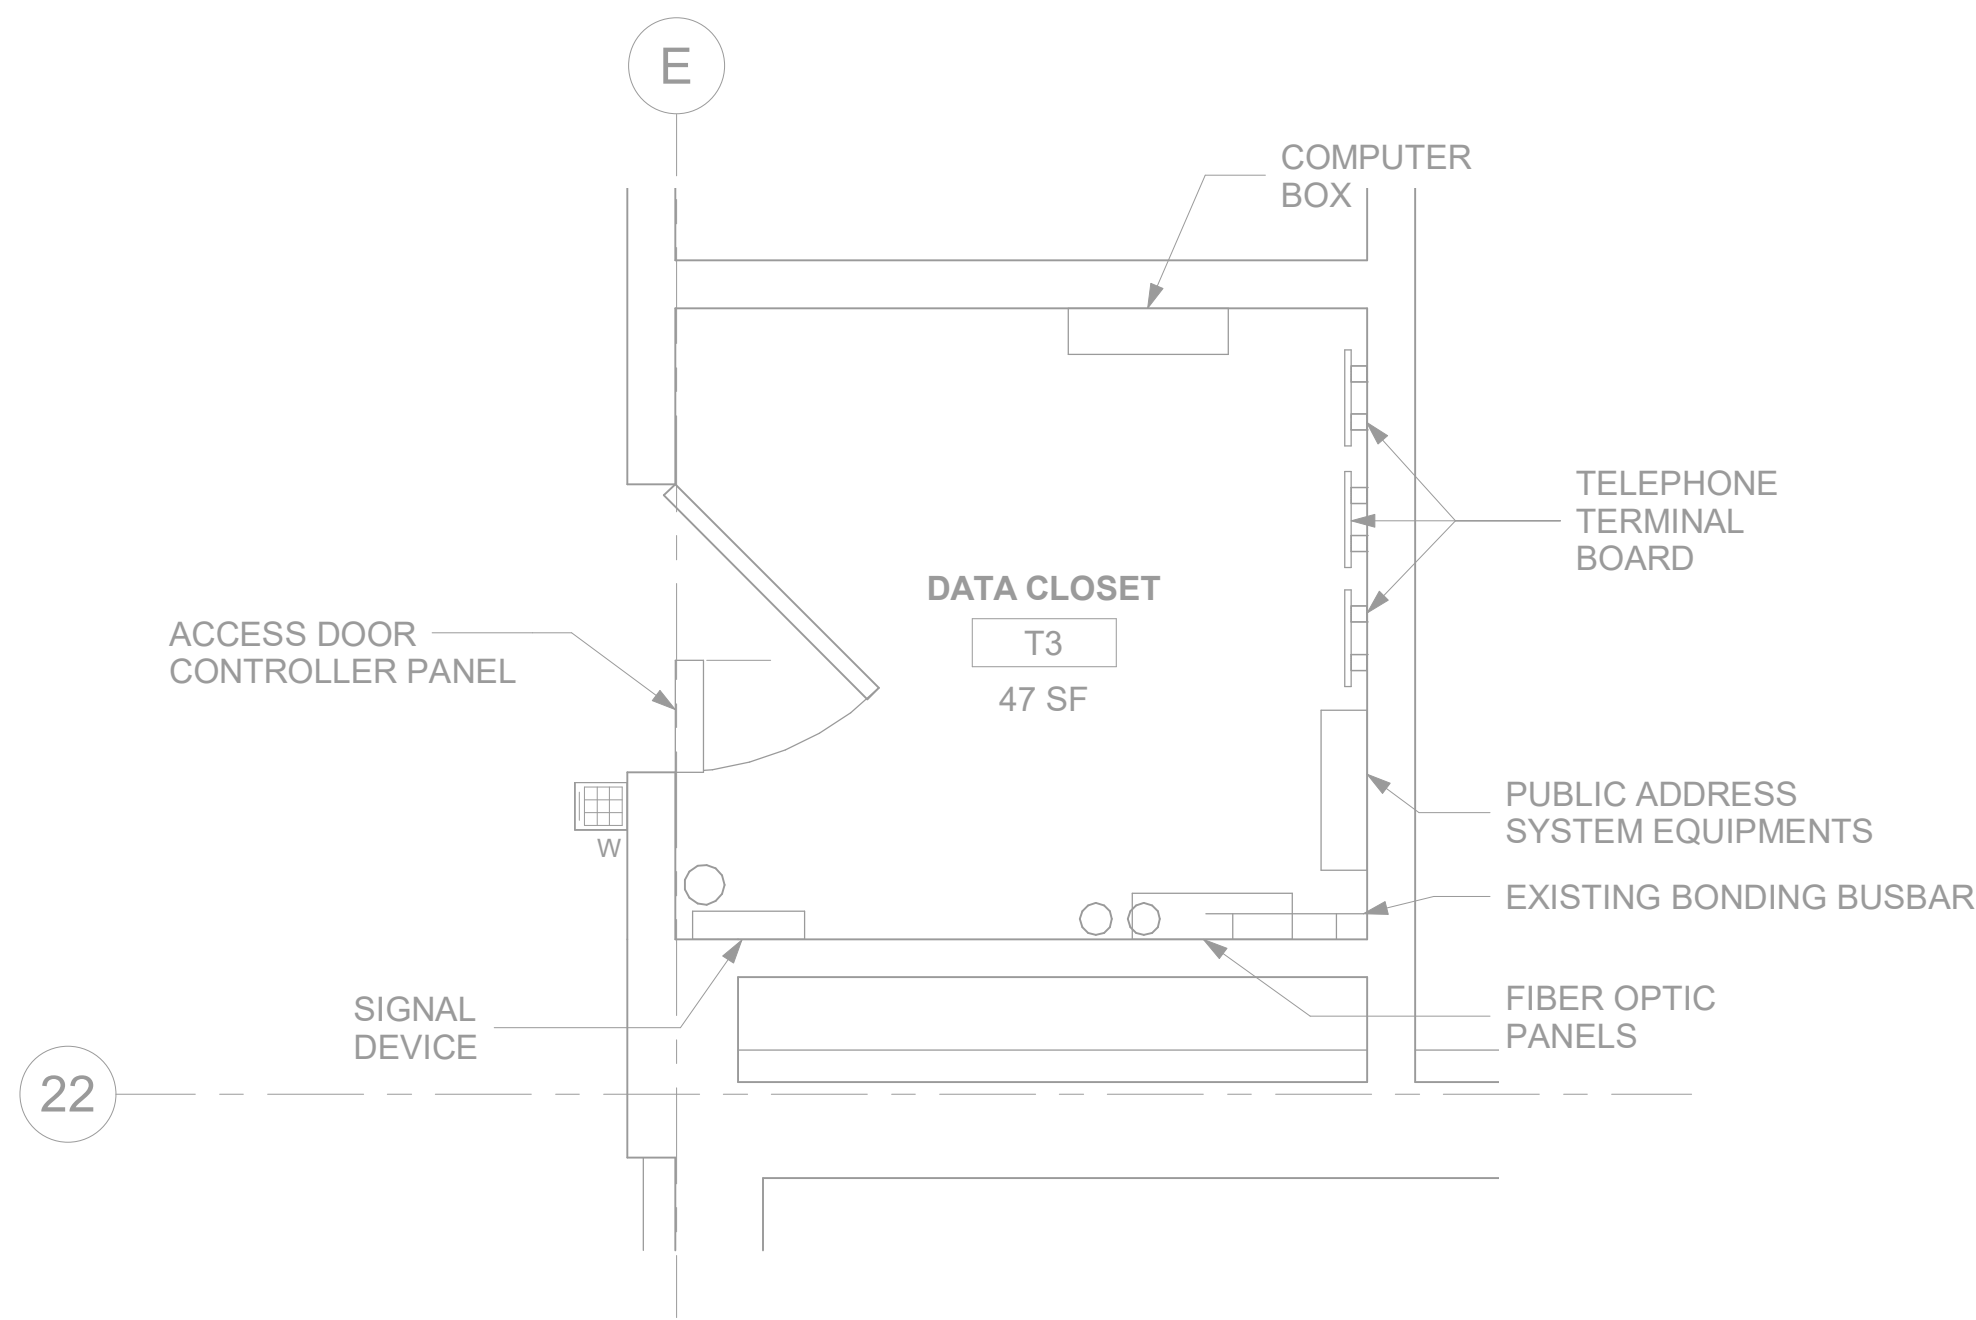

2 RM T3 - TELECOMMUNICATIONS PLAN
146TN101A 1/2" = 1'-0"

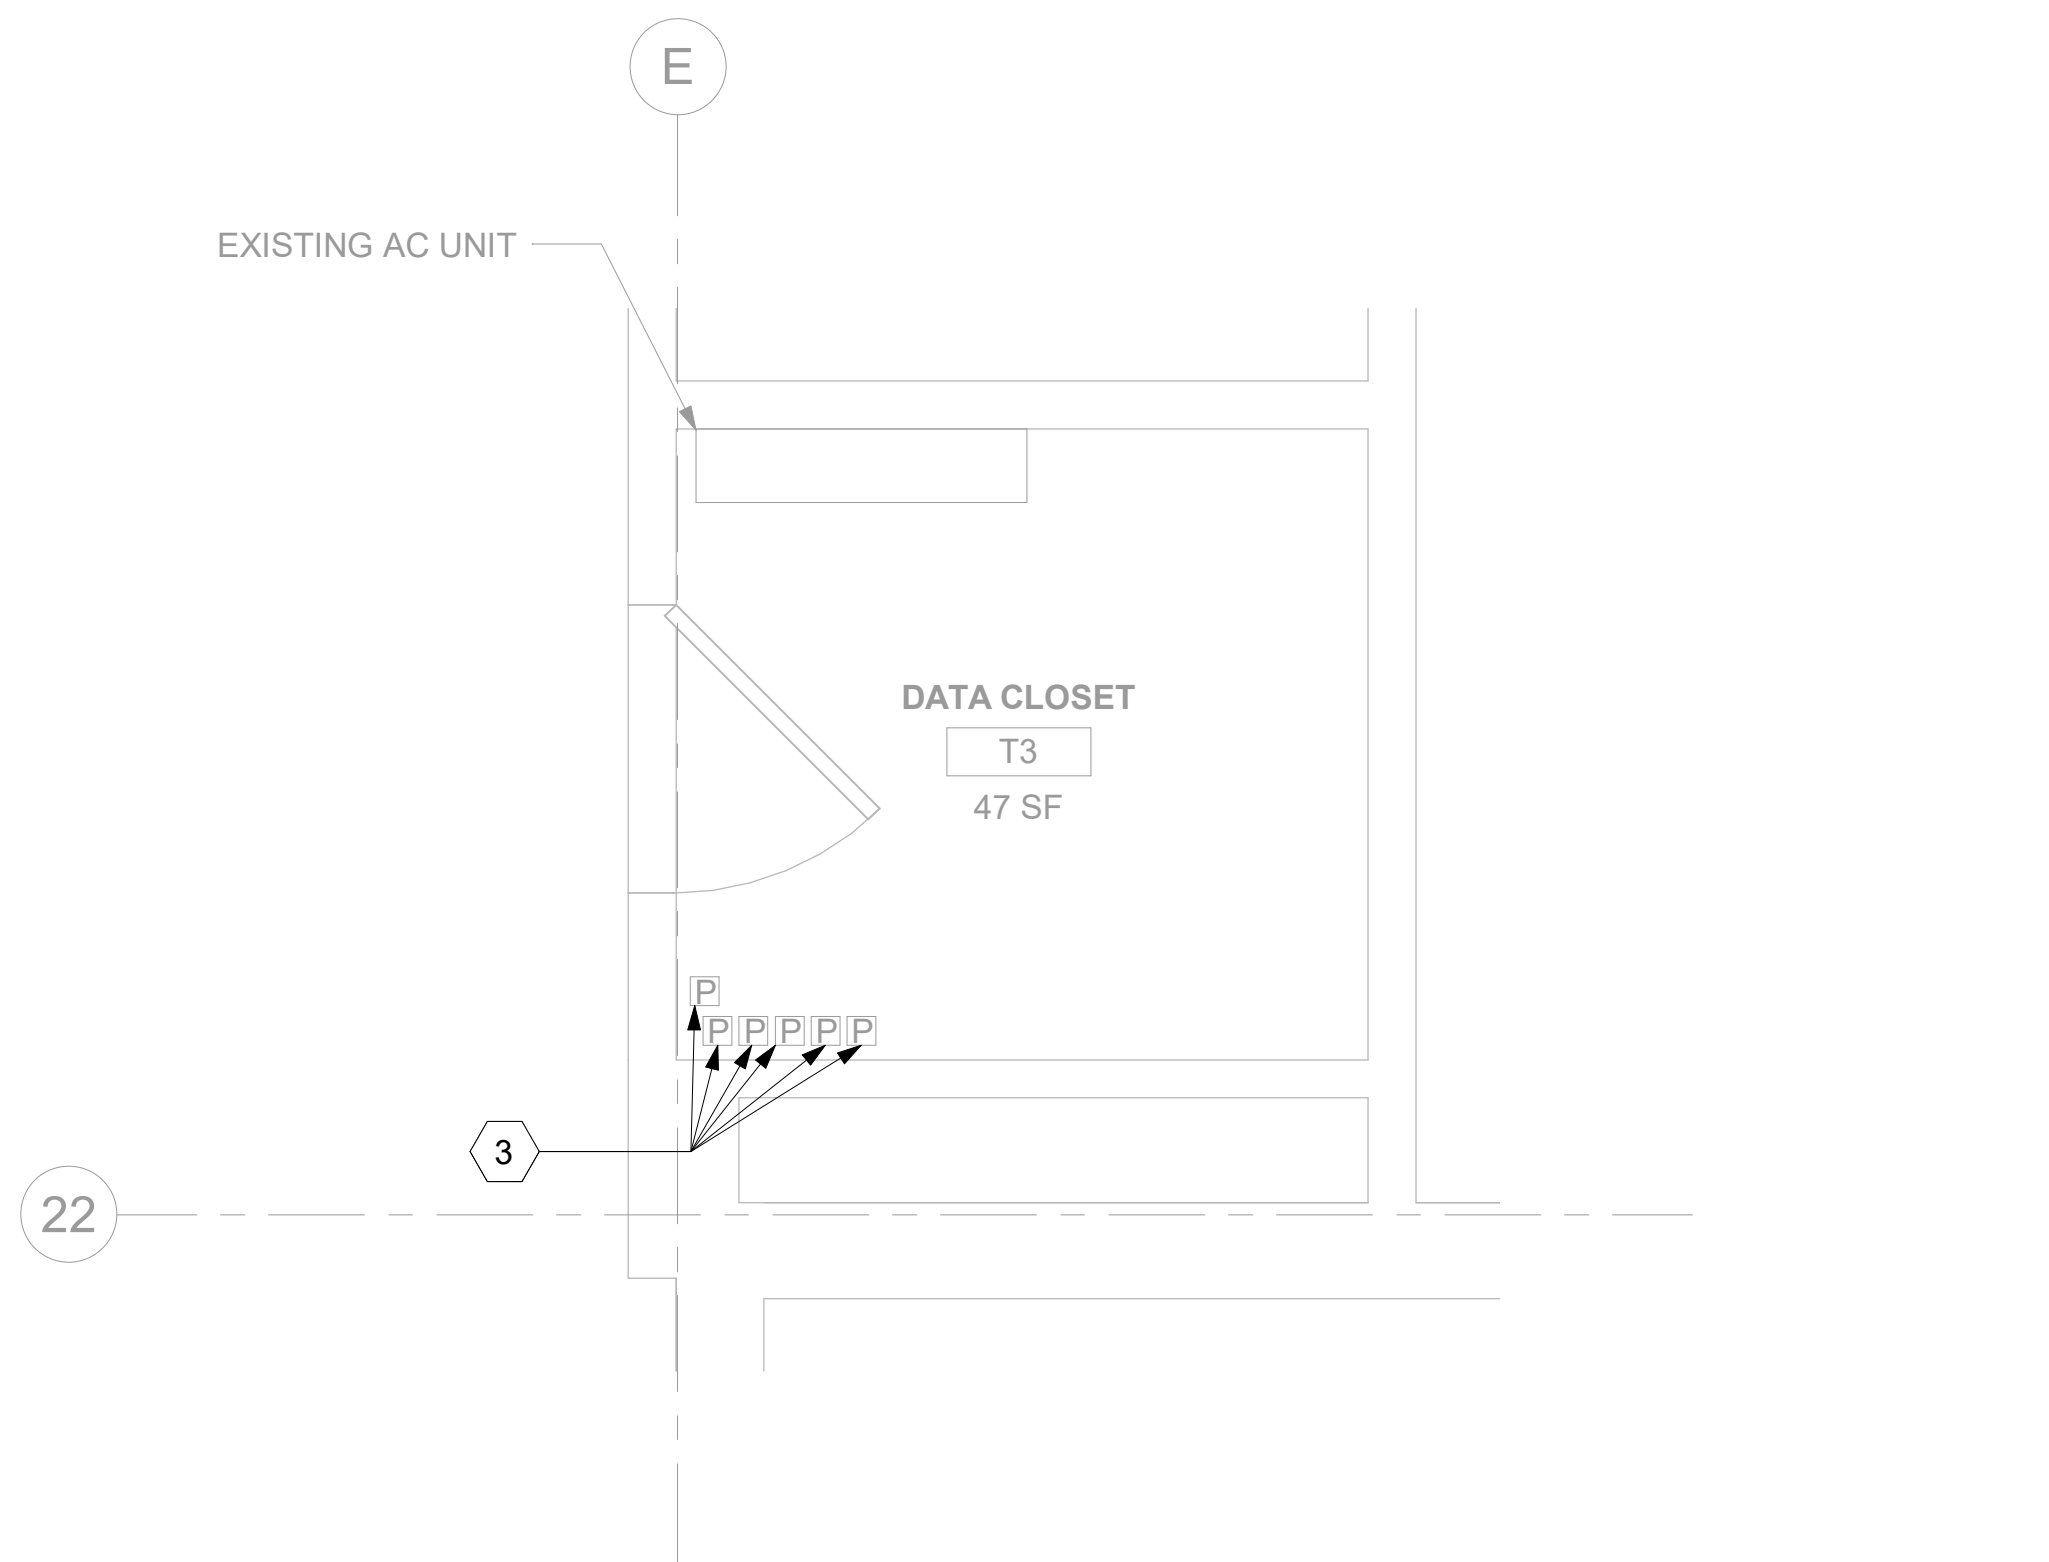

3 RM T3 - DEMOLITION OVERHEAD PLAN
146TN101A 1/2" = 1'-0"

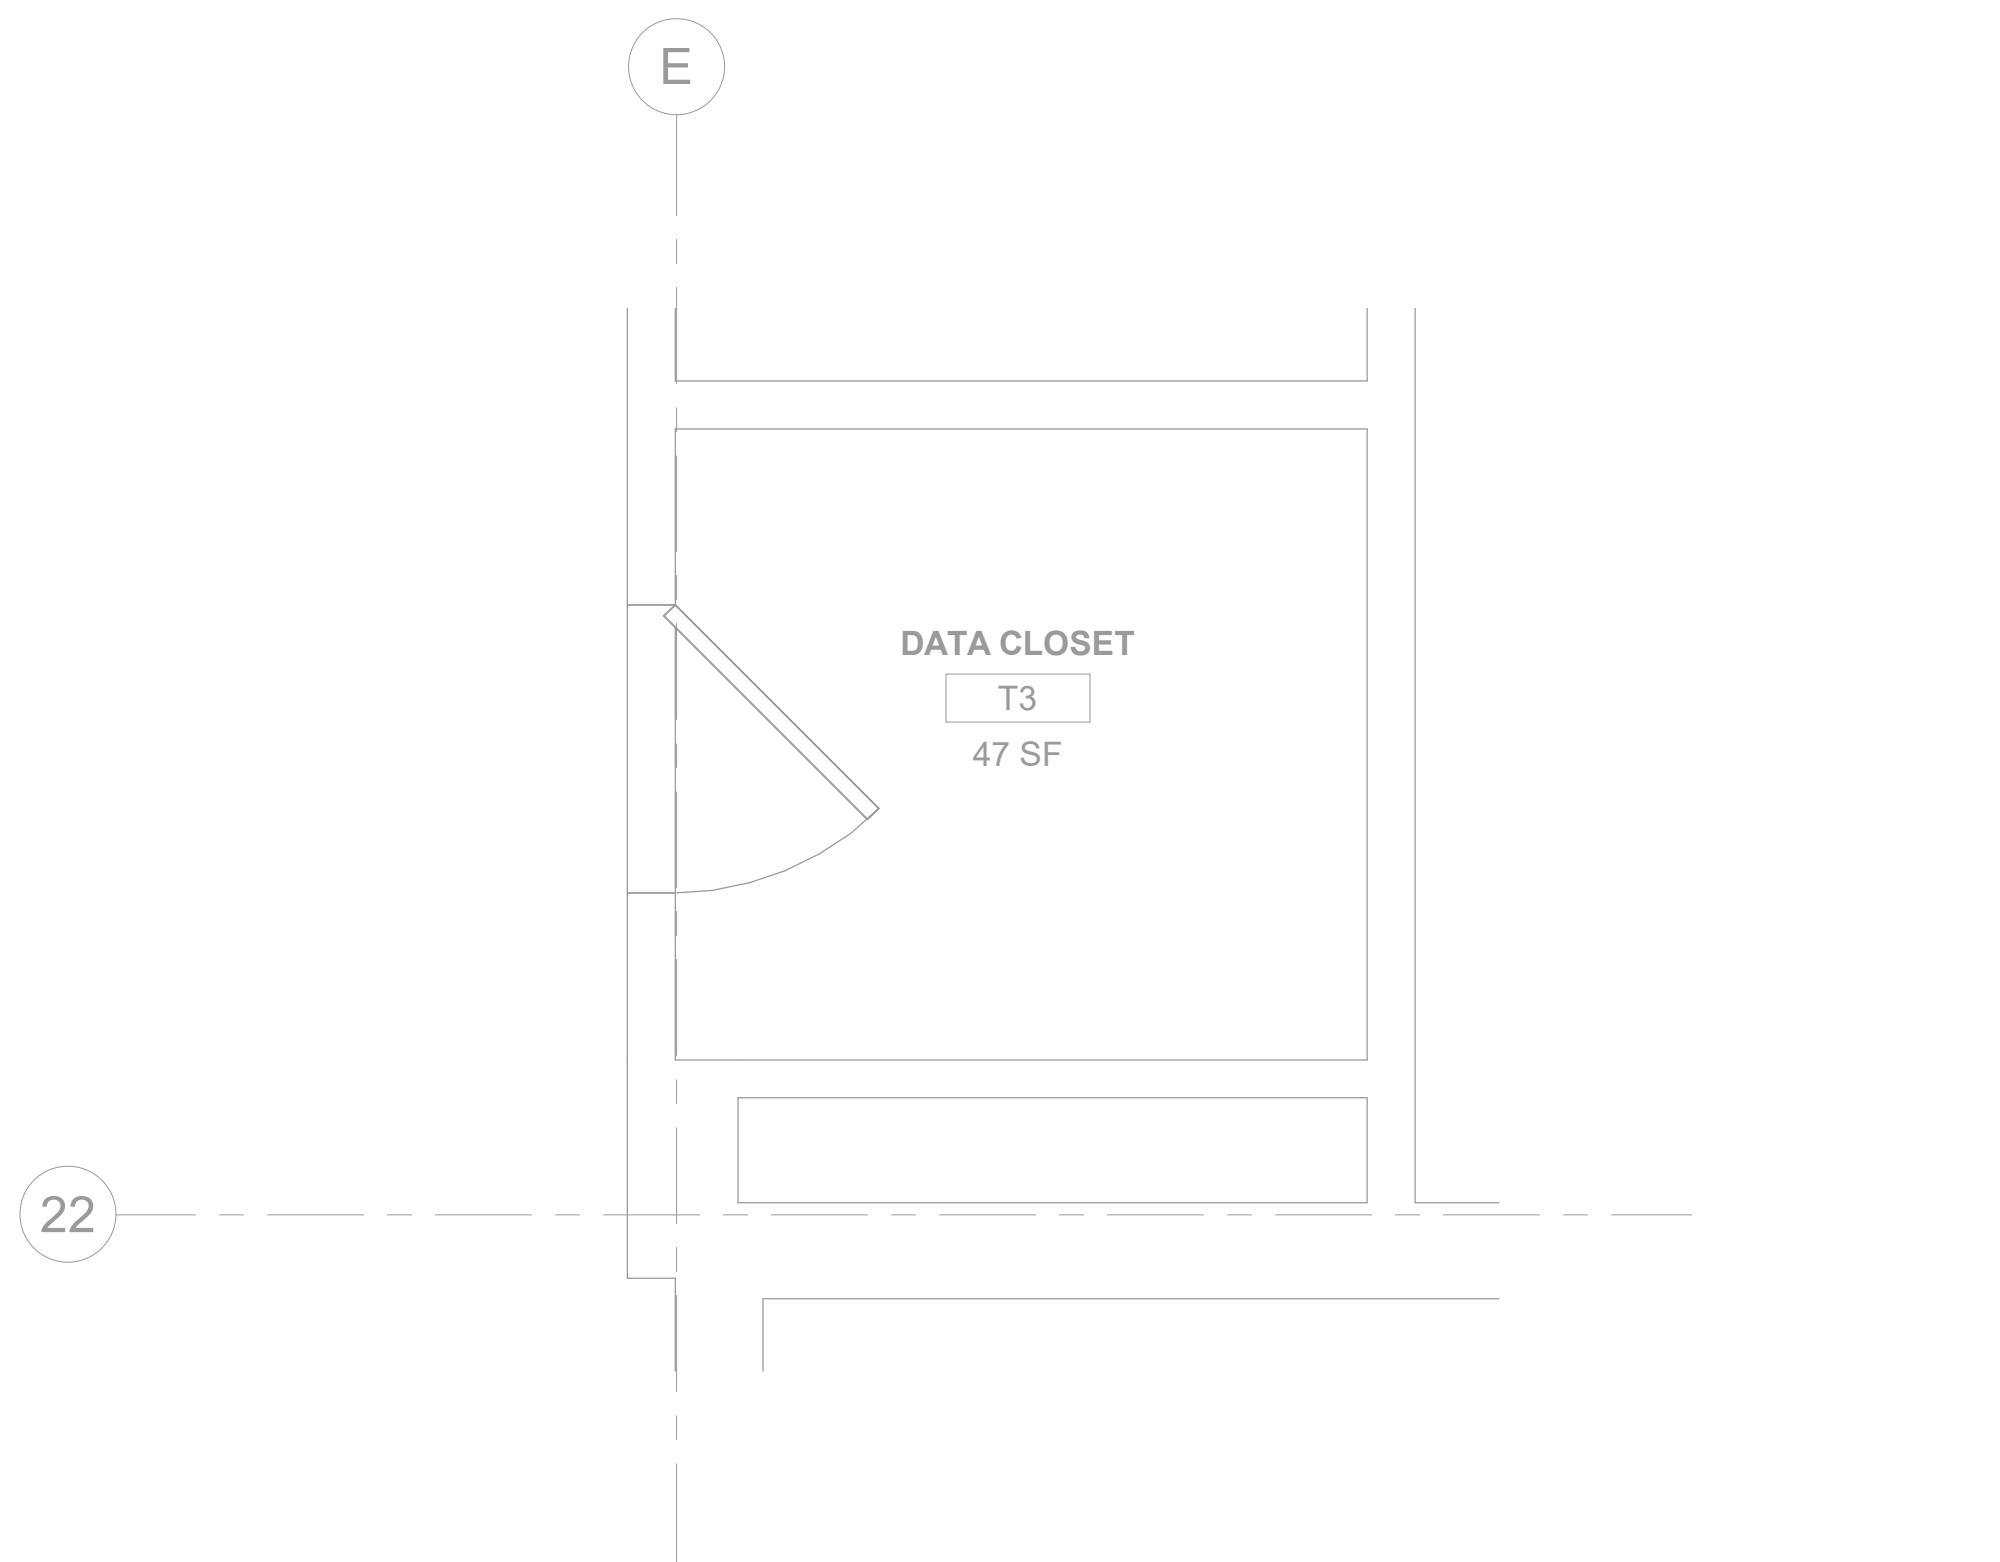

4 RM T3 - OVERHEAD PLAN
146TN101A 1/2" = 1'-0"


GENERAL NOTES

- PROTECT ALL EXISTING WORK FROM DAMAGE DURING CONSTRUCTION. ANY DAMAGED MATERIALS, SYSTEMS, COMPONENTS, FINISHES AND THE LIKE, SHALL BE REPAIRED OR REPLACED AT THE EXPENSE OF THE CONTRACTOR TO THE ACCEPTANCE OF THE OWNER.
- SEAL ALL INTERIOR WALL AND CEILING PENETRATIONS TO MATCH EXISTING FIRE RATING OR NEW FIRE RATING, IF REQUIRED. COORDINATE WITH ARCHITECTURAL DRAWINGS AS REQUIRED.
- ALL TELECOMMUNICATIONS CABLING CATEGORY 6 AND BELOW SHALL BE REMOVED AND REPLACED WITH CAT6A PORTS AND CABLE QUANTITIES INDICATED, UNLESS NOTED OTHERWISE.
- TELECOMMUNICATIONS CABLES SHALL BE ROUTED IN EXISTING PATHWAY VACATED BY EXISTING CABLING. PROVIDE RACEWAYS TO EXTEND TO ASSOCIATED TR.
- A TELECOMMUNICATIONS OUTLET UPGRADE SHALL INCLUDE, BUT IS NOT LIMITED TO REMOVING AND DISPOSING EXISTING DEVICES AND CABLES; PROVIDING ALL LABOR, MATERIALS, TOOLS, TEST INSTRUMENTS, AND CONSUMABLES REQUIRED FOR THE INSTALLATION, TERMINATION, TESTING, LABELING, AND CERTIFICATION OF A FULLY FUNCTIONAL CATEGORY 6A OUTLET WITH THE PORT QUANTITY INDICATED.
- WHERE NEW DATA OUTLETS ARE BEING PROVIDED AND EXISTING DATA OUTLET CURRENTLY DOES NOT EXIST, PROVIDE (1) 1" CONDUIT FROM NEW BACKBOX TO ACCESSIBLE CEILING SPACE TO SECURELY ROUTE DATA CABLING FROM OUTLET TO TR VIA CABLE TRAY. IF CABLE TRAY IS NON-EXISTENT, EXTEND RACEWAY FROM OUTLET TO TR AS REQUIRED.
- PROVIDE CONDUITS AND SLEEVES AS REQUIRED FOR ROUTING AND INSTALLATION OF HORIZONTAL AND BACKBONE CABLING. PROVIDE FIRE-STOP MATERIALS TO SEAL IN AND AROUND CONDUIT PER CODE. REFER TO ARCHITECTURAL DRAWINGS FOR PARTITION TYPES AND WALL HEIGHTS.
- ALL TELECOMMUNICATION ROOMS SHALL BE PROVIDED WITH FIRE-RATED PLYWOOD BACKBOARDS. REFERENCE EXACT PLACEMENTS WITH ARCHITECTURE DRAWINGS AS REQUIRED.
- ANY LIVE SYSTEMS IN DEMO'D TR'S MUST REMAIN LIVE. CONTRACTOR TO COORDINATE WITH THE STATION TO IDENTIFY SYSTEMS THAT ARE LIVE. IF SYSTEMS ARE LIVE; INSTALL NEW CABLE FROM DEMO'D TR TO NEW TR. REFER TO DETAIL '3' ON TN506.

KEY NOTES

- EXISTING DATA RACK TO BE DECOMMISSIONED BY VA. CONTRACTOR SHALL COORDINATE WITH VA AS REQUIRED.
- EXISTING VERTICAL CABLING SLEEVES TO BE PRESERVED. EXISTING FIBER OPTIC AND/OR EXISTING VERTICAL CABLING RELATED TO EXISTING TR RACKS TO BE DEMOLISHED.
- EXISTING PENETRATIONS WITH CABLING TO BE REMOVED. CONTRACTOR SHALL PATCH AND FIREPROOF OPENINGS. COORDINATE WITH ARCHITECTURAL DRAWINGS AND SPECIFICATIONS.

KEY PLAN

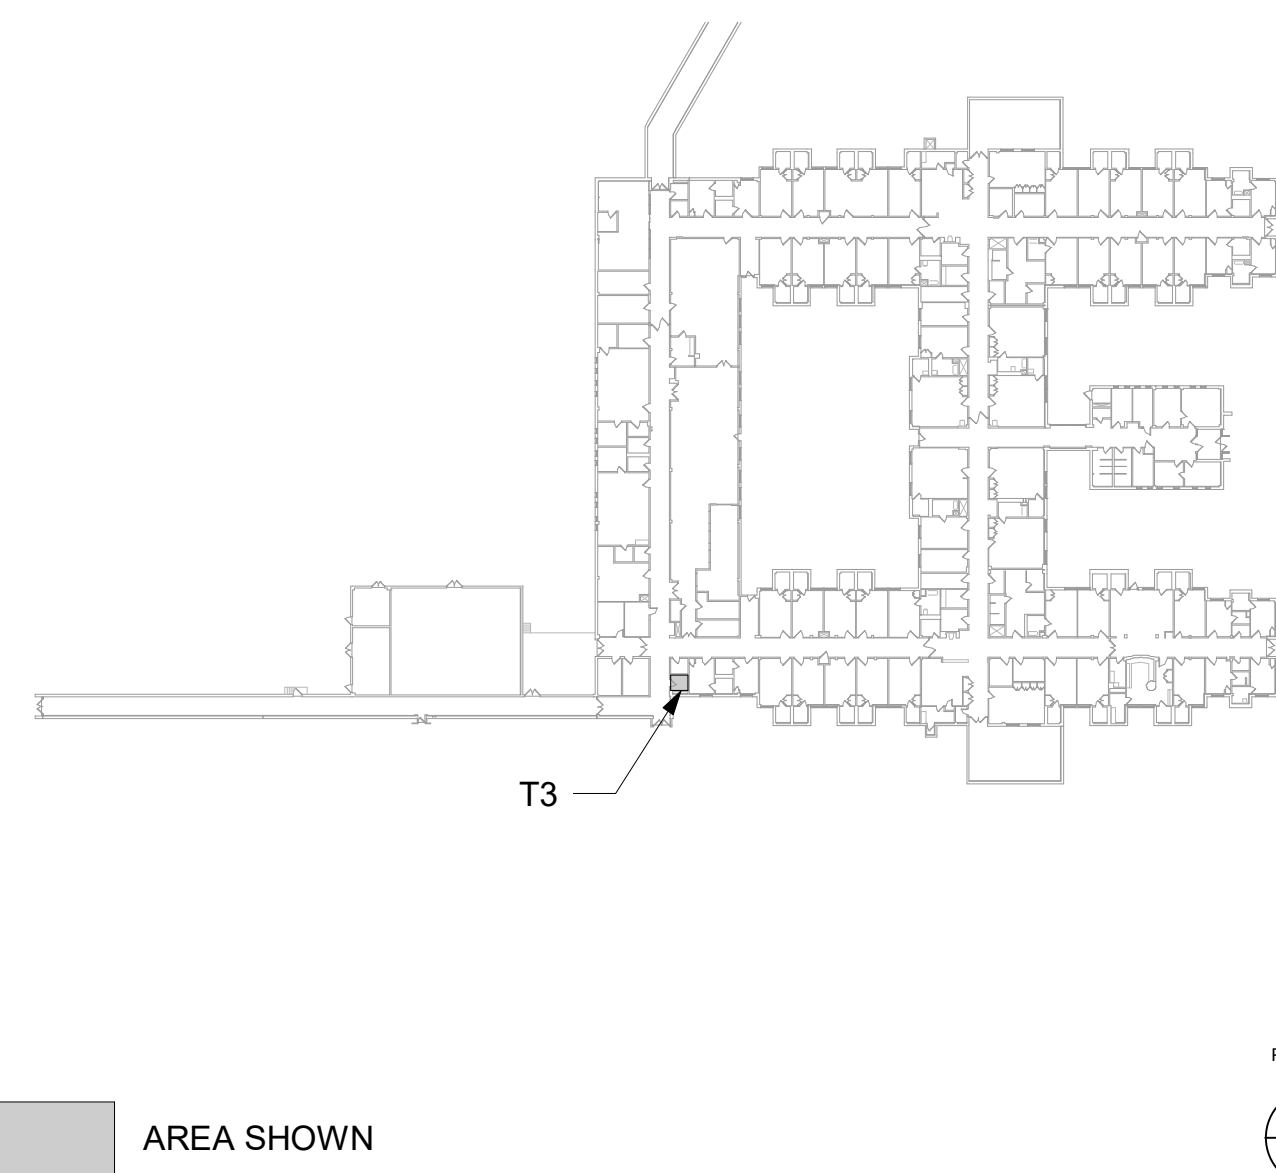

Revisions:		CONSULTANT	ARCHITECT/ENGINEER OF RECORD	STAMP	Drawing Title	Phase	Project Title	Project Number
Date:		ENGINEERING DISCIPLINE:	A/E:		BLDG 146 - LEVEL 01 - ENLARGED TELECOMMUNICATIONS PLANS	100% CONSTRUCTION DOCUMENTS	EHRM INFRASTRUCTURE UPGRADES - HAMPTON	590-22-700
			SPEES DESIGN BUILD 23830 PACIFIC HIGHWAY S. SUITE 203 KENT, WA 98032		Approved:	FULLY SPRINKLERED	Location HAMPTON VA MEDICAL CENTER, HAMPTON, VIRGINIA	Building Number 146
				Office of Construction and Facilities Management VA U.S. Department of Veterans Affairs			Issue Date 07/18/2025	Drawn BCL/GPB
							Checked KG	Drawn BCL/GPB
								Project Number 146TN401e
								602 of 713

A


B

C



D

E



F

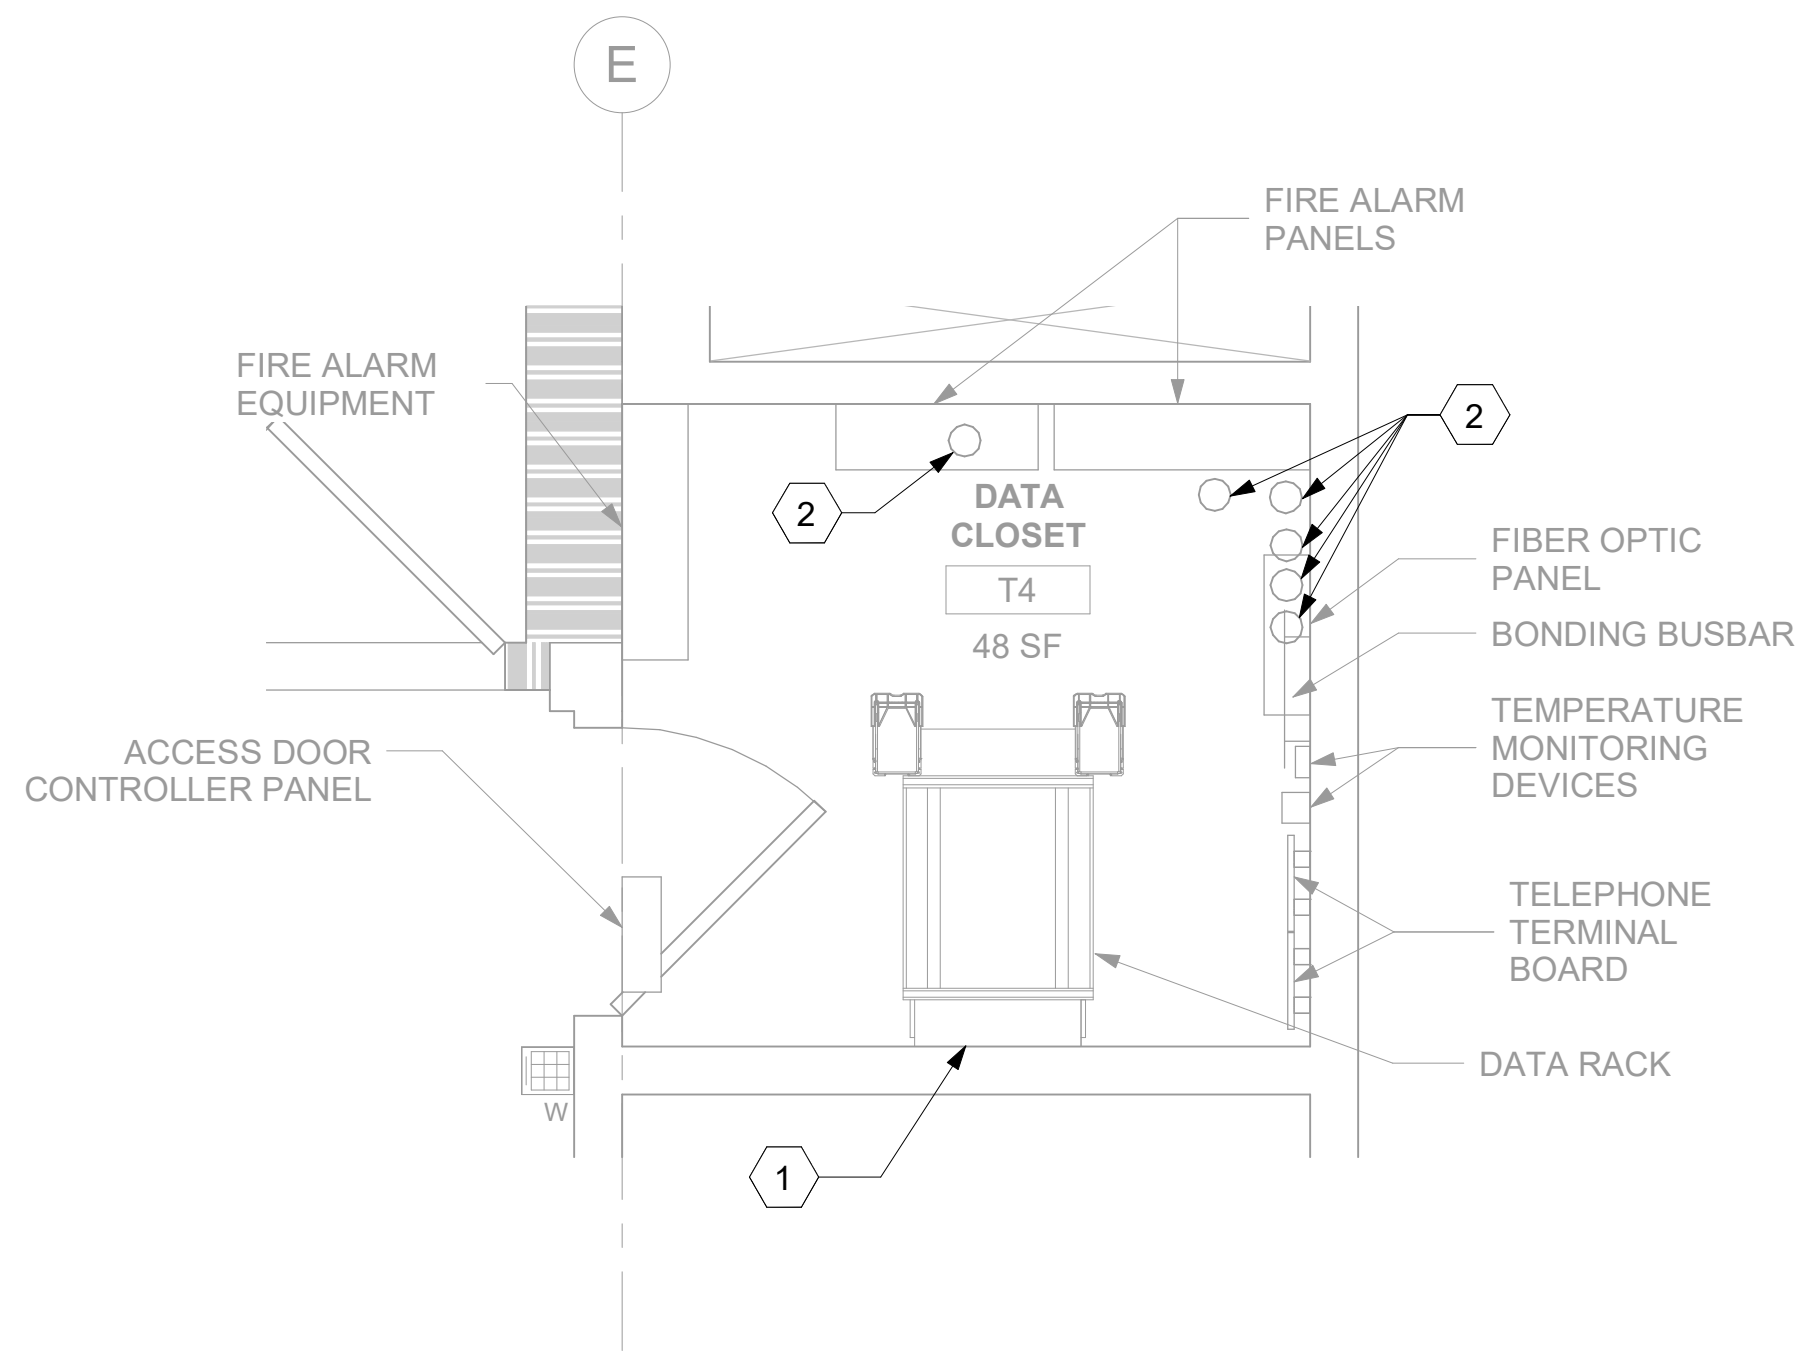



1 RM T4 - DEMOLITION FLOOR PLAN
146TN101A 1/2" = 1'-0"

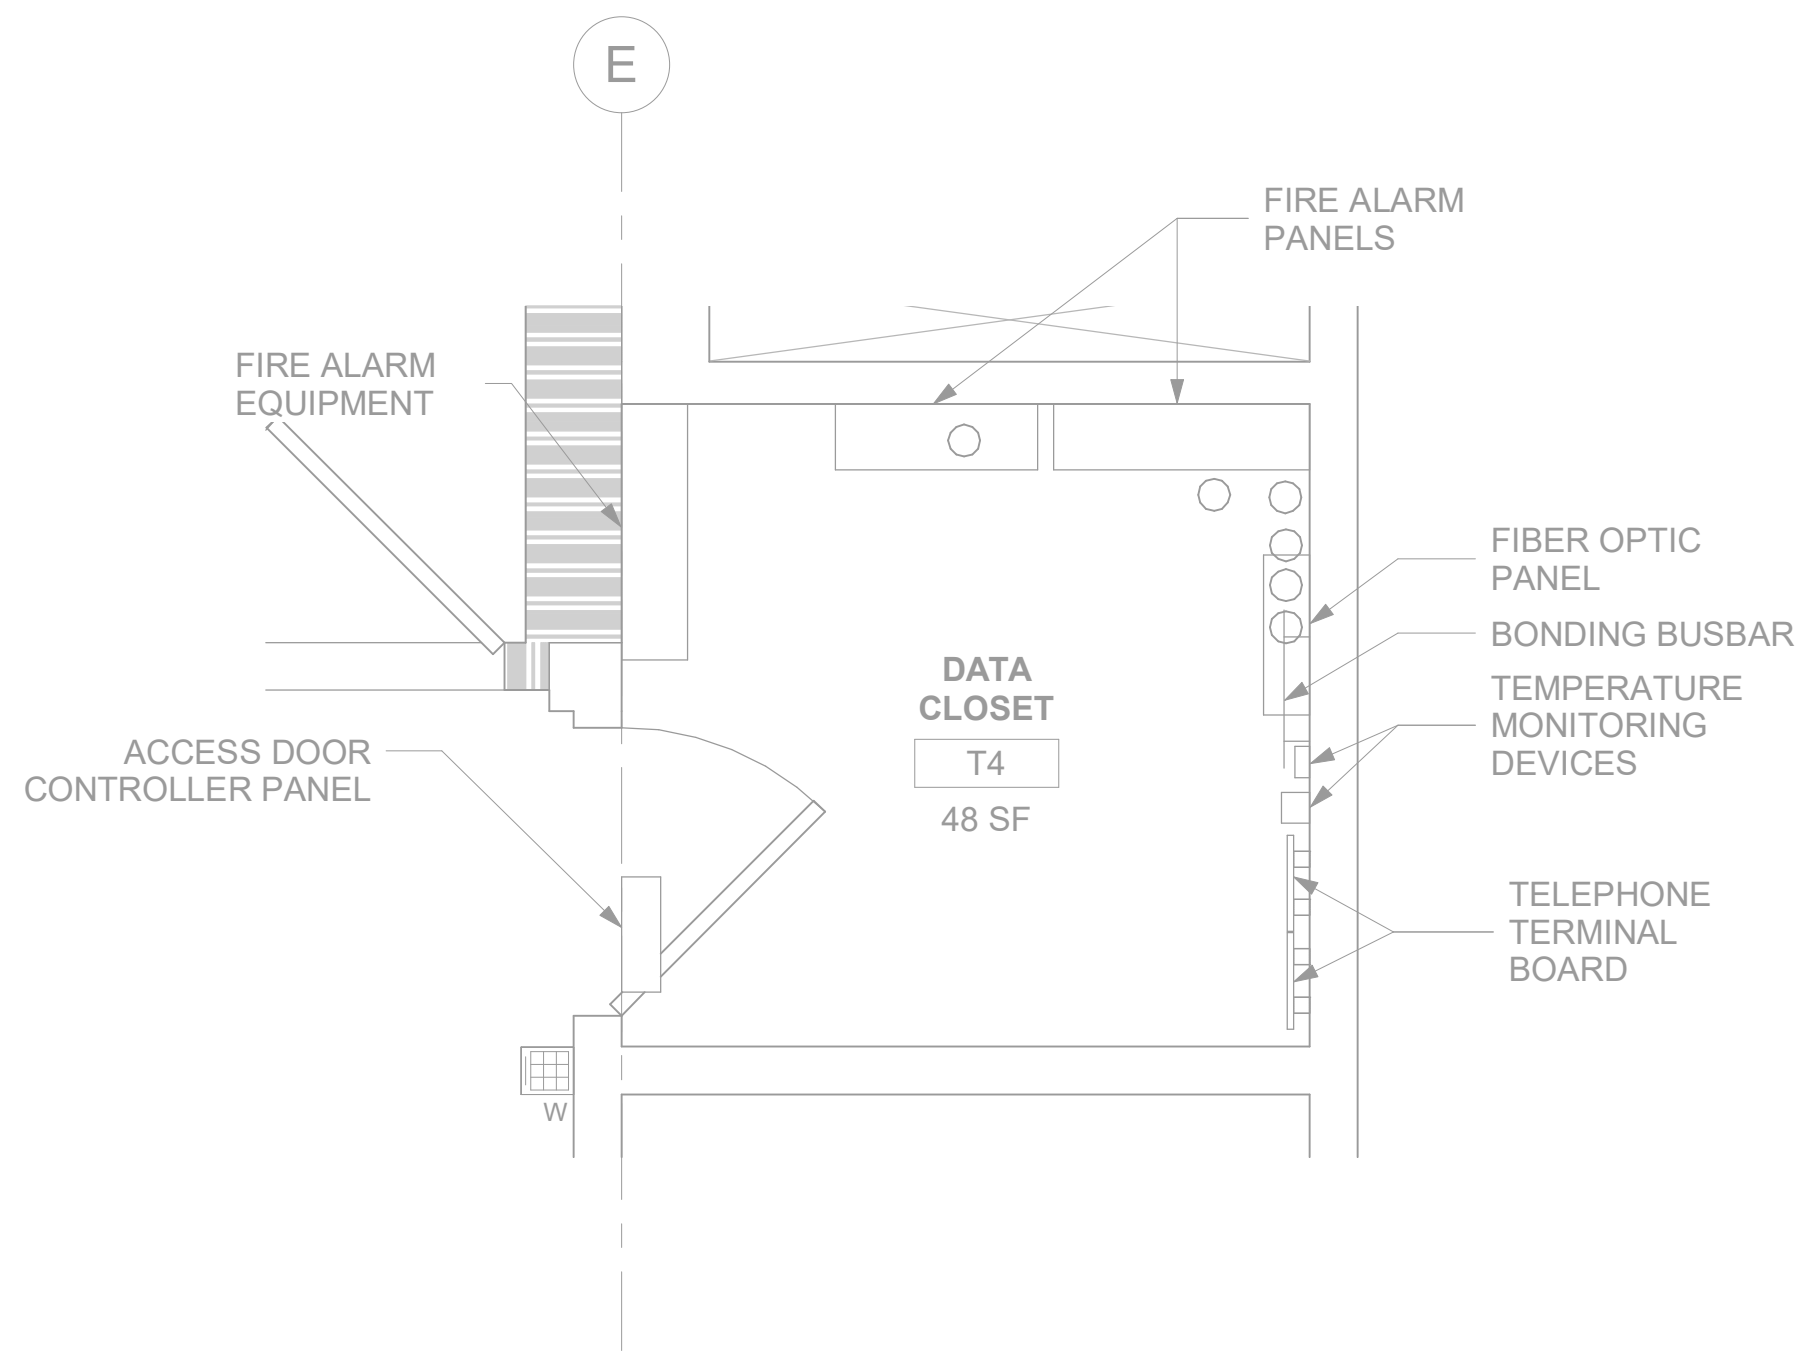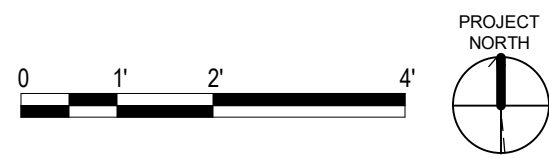


2 RM T4 - TELECOMMUNICATIONS PLAN
146TN101A 1/2" = 1'-0"

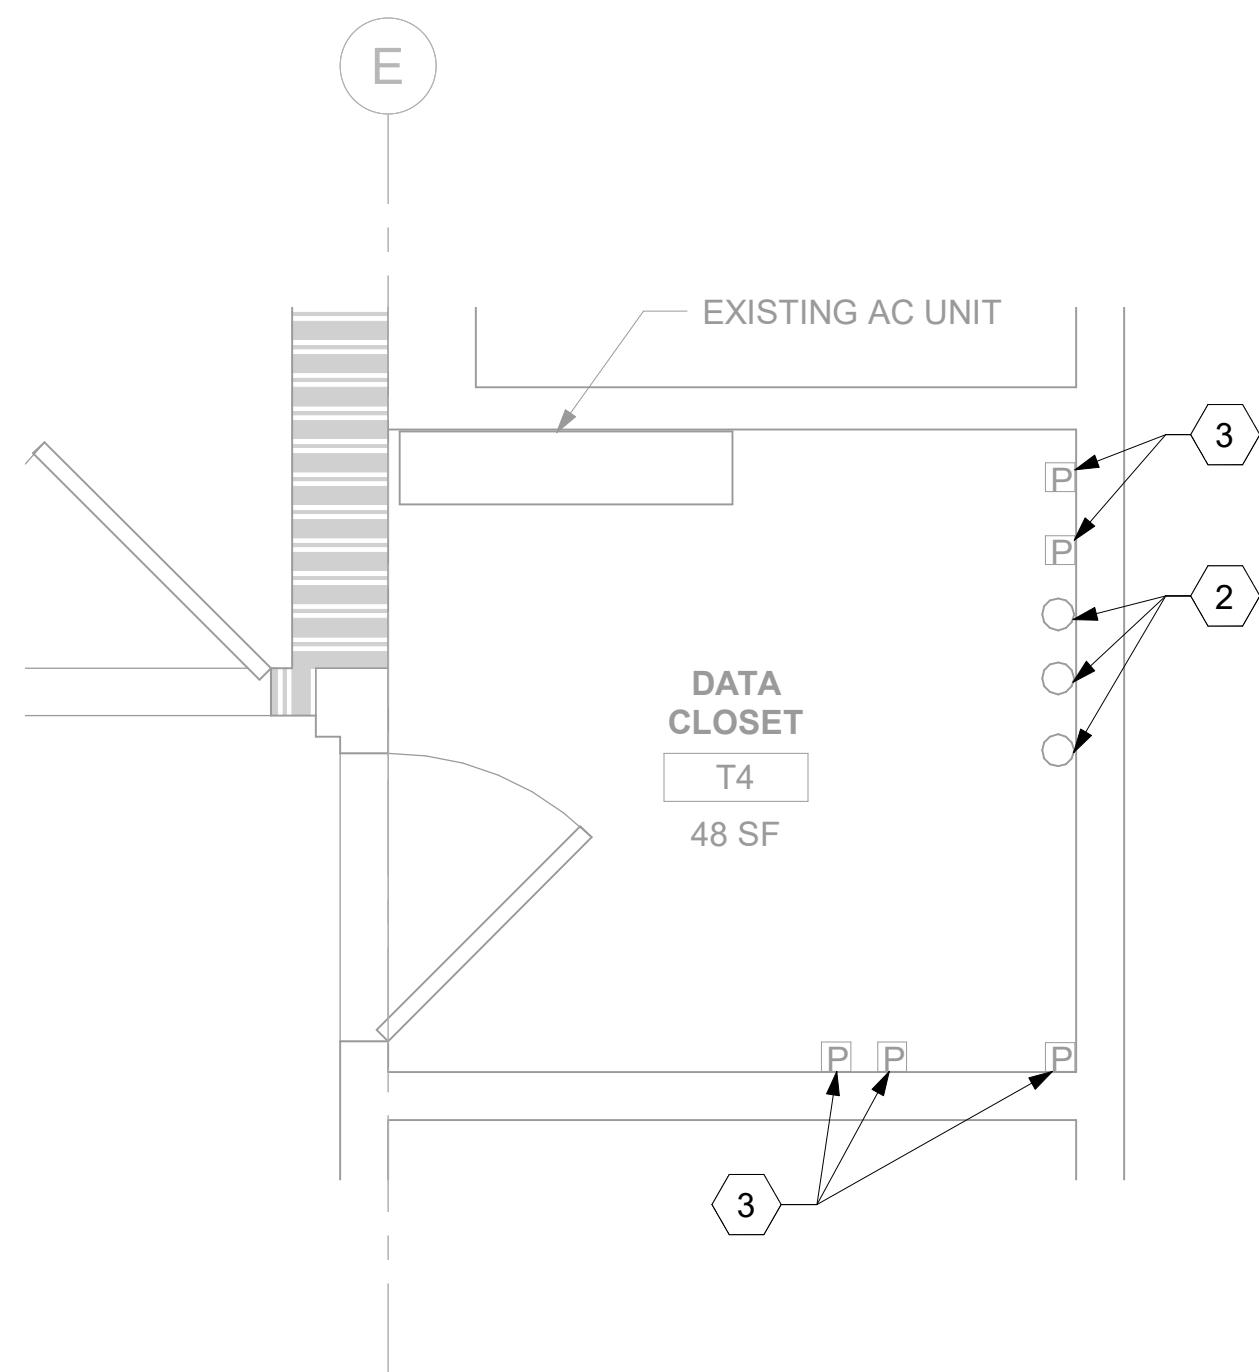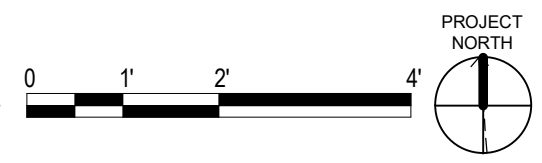

3 RM T4 - DEMOLITION OVERHEAD PLAN
146TN101A 1/2" = 1'-0"

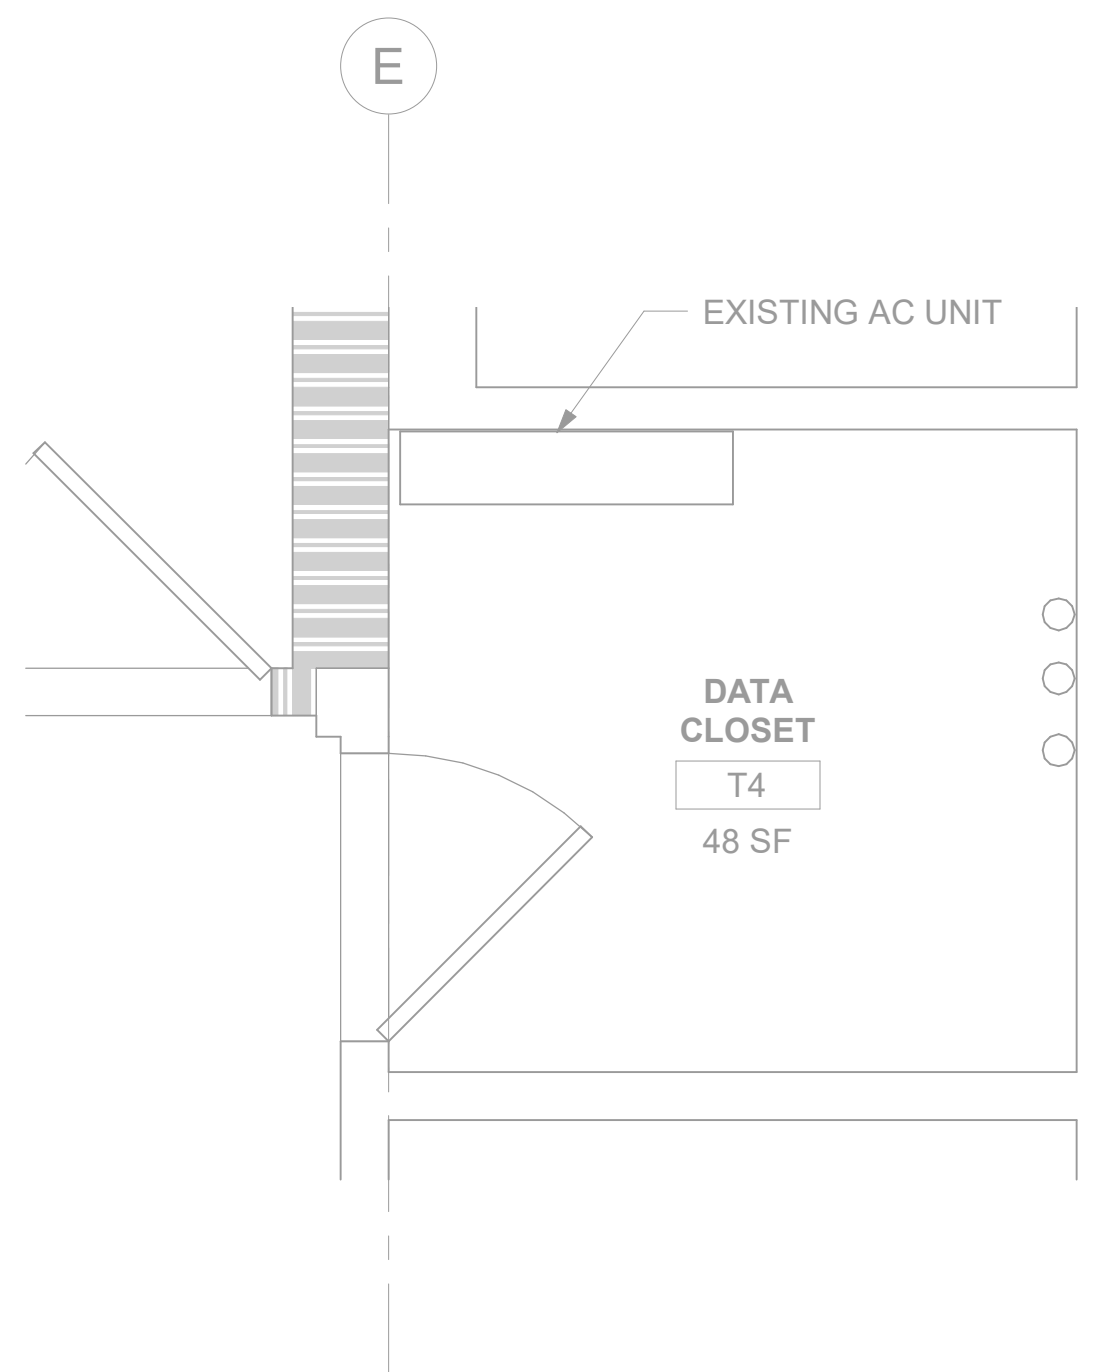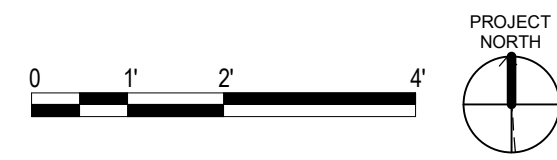

4 RM T4 - OVERHEAD PLAN
146TN101A 1/2" = 1'-0"

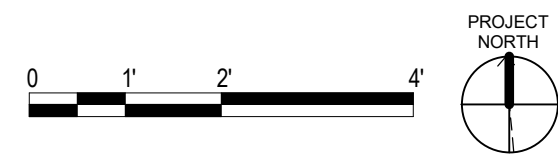


GENERAL NOTES

1. PROTECT ALL EXISTING WORK FROM DAMAGE DURING CONSTRUCTION. ANY DAMAGED MATERIALS, SYSTEMS, COMPONENTS, FINISHES AND THE LIKE, SHALL BE REPAIRED OR REPLACED AT THE EXPENSE OF THE CONTRACTOR TO THE ACCEPTANCE OF THE OWNER.
2. SEAL ALL INTERIOR WALL AND CEILING PENETRATIONS TO MATCH EXISTING FIRE RATING OR NEW FIRE RATING, IF REQUIRED. COORDINATE WITH ARCHITECTURAL DRAWINGS AS REQUIRED.
3. ALL TELECOMMUNICATIONS CABLING CATEGORY 6 AND BELOW SHALL BE REMOVED AND REPLACED WITH CAT6A PORTS AND CABLE QUANTITIES INDICATED, UNLESS NOTED OTHERWISE.
4. TELECOMMUNICATIONS CABLES SHALL BE ROUTED IN EXISTING PATHWAY VACATED BY EXISTING CABLING. PROVIDE RACEWAYS TO EXTEND TO ASSOCIATED TR.
5. A TELECOMMUNICATIONS OUTLET UPGRADE SHALL INCLUDE, BUT IS NOT LIMITED TO REMOVING AND DISPOSING EXISTING DEVICES AND CABLES; PROVIDING ALL LABOR, MATERIALS, TOOLS, TEST INSTRUMENTS, AND CONSUMABLES REQUIRED FOR THE INSTALLATION, TERMINATION, TESTING, LABELING, AND CERTIFICATION OF A FULLY FUNCTIONAL CATEGORY 6A OUTLET WITH THE PORT QUANTITY INDICATED.
6. WHERE NEW DATA OUTLETS ARE BEING PROVIDED AND EXISTING DATA OUTLET CURRENTLY DOES NOT EXIST, PROVIDE (1) 1" CONDUIT FROM NEW BACKBOX TO ACCESSIBLE CEILING SPACE TO SECURELY ROUTE DATA CABLING FROM OUTLET TO TR VIA CABLE TRAY. IF CABLE TRAY IS NON-EXISTENT, EXTEND RACEWAY FROM OUTLET TO TR AS REQUIRED.
7. PROVIDE CONDUITS AND SLEEVES AS REQUIRED FOR ROUTING AND INSTALLATION OF HORIZONTAL AND BACKBONE CABLING. PROVIDE FIRE-STOP MATERIALS TO SEAL IN AND AROUND CONDUIT PER CODE. REFER TO ARCHITECTURAL DRAWINGS FOR PARTITION TYPES AND WALL HEIGHTS.
8. ALL TELECOMMUNICATION ROOMS SHALL BE PROVIDED WITH FIRE-RATED PLYWOOD BACKBOARDS. REFERENCE EXACT PLACEMENTS WITH ARCHITECTURE DRAWINGS AS REQUIRED.
9. ANY LIVE SYSTEMS IN DEMO'D TR'S MUST REMAIN LIVE. CONTRACTOR TO COORDINATE WITH THE STATION TO IDENTIFY SYSTEMS THAT ARE LIVE. IF SYSTEMS ARE LIVE, INSTALL NEW CABLE FROM DEMO'D TR TO NEW TR. REFER TO DETAIL '3' ON TN506.

KEY NOTES

- 1 EXISTING DATA RACK TO BE DECOMMISSIONED BY VA. CONTRACTOR SHALL COORDINATE WITH VA AS REQUIRED.
- 2 EXISTING VERTICAL CABLING SLEEVES TO BE PRESERVED. EXISTING FIBER OPTIC AND/OR EXISTING VERTICAL CABLING RELATED TO EXISTING TR RACKS TO BE DEMOLISHED.
- 3 EXISTING PENETRATIONS WITH CABLING TO BE REMOVED. CONTRACTOR SHALL PATCH AND FIREPROOF OPENINGS. COORDINATE WITH ARCHITECTURAL DRAWINGS AND SPECIFICATIONS.

KEY PLAN

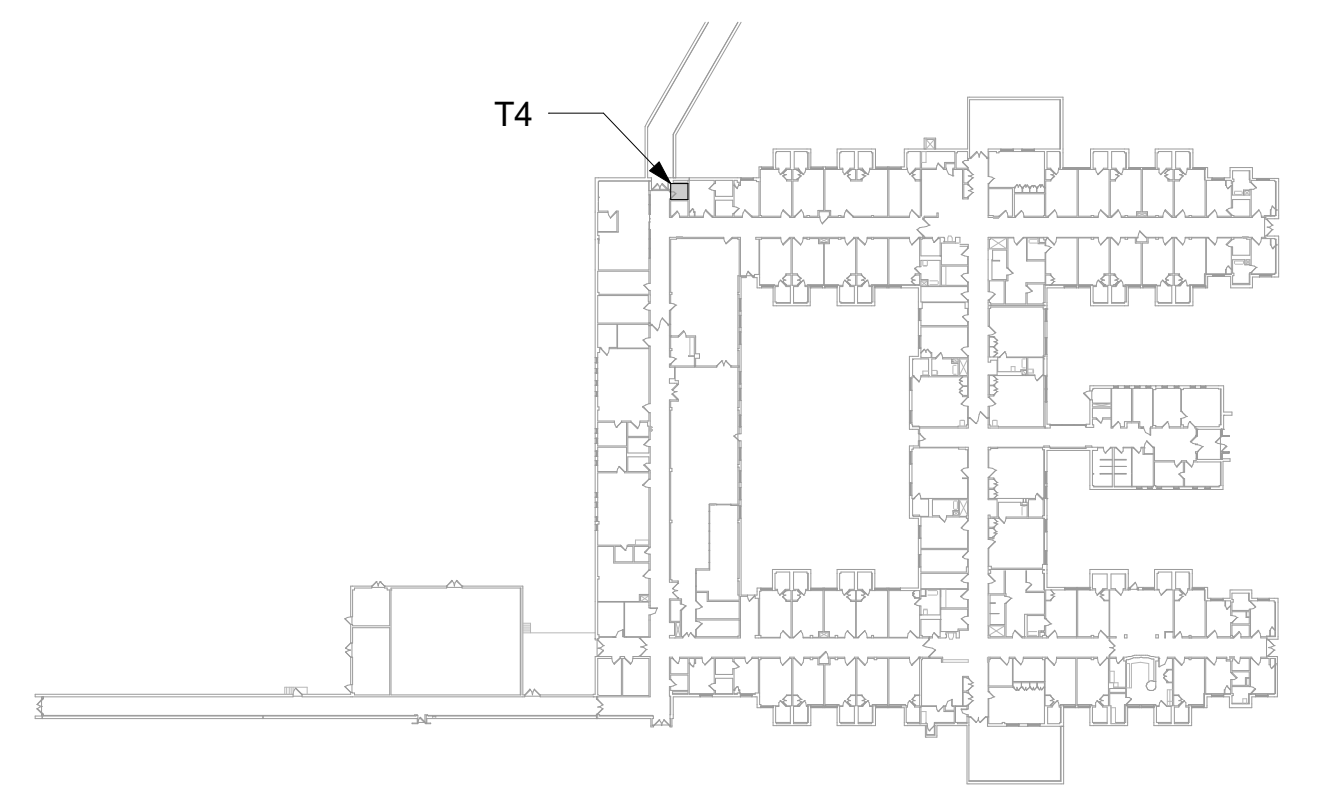

AREA SHOWN



Revisions:	Date:

CONSULTANT
ENGINEERING DISCIPLINE:

ARCHITECT/ENGINEER OF RECORD

A/E:
SPEES DESIGN BUILD
23830 PACIFIC HIGHWAY S. SUITE 203
KENT, WA 98032



STAMP



Office of
Construction
and Facilities
Management



U.S. Department
of Veterans Affairs

Drawing Title
BLDG 146 - LEVEL 01 - ENLARGED
TELECOMMUNICATIONS PLANS

Approved:

Phase
100% CONSTRUCTION
DOCUMENTS

FULLY SPRINKLERED

Project Title
EHRM INFRASTRUCTURE
UPGRADES - HAMPTON

Location
HAMPTON VA MEDICAL CENTER, HAMPTON, VIRGINIA

Issue Date
07/18/2025

Checked
KG

Drawn
BCL/GPB

Project Number
590-22-700

Building Number
146

Drawing Number
146TN401f

603 of 713

BM 360/599-22-700
Washington EHRMEE - BLDG
146-1A

15/07/2025 8:33:43 am

VA FORM 08 - 6231

Revisions:	Date:

CONSULTANT
ENGINEERING DISCIPLINE:

ARCHITECT/ENGINEER OF RECORD
A/E: SPEES DESIGN BUILD 23830 PACIFIC HIGHWAY S. SUITE 203 KENT, WA 98032


STAMP


Office of Construction and Facilities Management
 U.S. Department of Veterans Affairs

Drawing Title BLDG 146 - LEVEL 01 - ENLARGED TELECOMMUNICATIONS PLANS
Approved:

Phase 100% CONSTRUCTION DOCUMENTS
FULLY SPRINKLERED

Project Title EHRM INFRASTRUCTURE UPGRADES - HAMPTON
Location HAMPTON VA MEDICAL CENTER, HAMPTON, VIRGINIA
Issue Date 07/18/2025
Checked KG
Drawn BCL/GPB

Project Number 590-22-700
Building Number 146
Drawing Number 146TN401g
604 of 713

BM 360/599-22-700
Washington EHRMEE - BLDG
148/1A
15/07/2025 11:10:19 am

VA FORM 08 - 6231

CONSULTANT

ENGINEERING DISCIPLINE:

ARCHITECT/ENGINEER OF RECORD

A/E:
SPEES DESIGN BUILD
23830 PACIFIC HIGHWAY S. SUITE 203
KENT, WA 98032



STAMP



Office of
Construction
and Facilities
Management



U.S. Department
of Veterans Affairs

Drawing Title

BLDG 148 - LEVEL 01 - ENLARGED
TELECOMMUNICATIONS PLANS

Approved:

Phase

100% CONSTRUCTION
DOCUMENTS

FULLY SPRINKLERED

Project Title

EHRM INFRASTRUCTURE
UPGRADES - HAMPTON

Location

HAMPTON VA MEDICAL CENTER, HAMPTON, VIRGINIA

Issue Date

07/18/2025

Checked

KG

Drawn

BCL/GPB

Project Number

590-22-700

Building Number

148

Drawing Number

148TN401a

605 of 713


GENERAL NOTES

- PROTECT ALL EXISTING WORK FROM DAMAGE DURING CONSTRUCTION. ANY DAMAGED MATERIALS, SYSTEMS, COMPONENTS, FINISHES AND THE LIKE, SHALL BE REPAIRED OR REPLACED AT THE EXPENSE OF THE CONTRACTOR TO THE ACCEPTANCE OF THE OWNER.
- SEAL ALL INTERIOR WALL AND CEILING PENETRATIONS TO MATCH EXISTING FIRE RATING OR NEW FIRE RATING, IF REQUIRED. COORDINATE WITH ARCHITECTURAL DRAWINGS AS REQUIRED.
- ALL TELECOMMUNICATIONS CABLING CATEGORY 6 AND BELOW SHALL BE REMOVED AND REPLACED WITH CAT6A PORTS AND CABLE QUANTITIES INDICATED, UNLESS NOTED OTHERWISE.
- TELECOMMUNICATIONS CABLES SHALL BE ROUTED IN EXISTING PATHWAY VACATED BY EXISTING CABLING. PROVIDE RACEWAYS TO EXTEND TO ASSOCIATED TR.
- A TELECOMMUNICATIONS OUTLET UPGRADE SHALL INCLUDE, BUT IS NOT LIMITED TO REMOVING AND DISPOSING EXISTING DEVICES AND CABLES; PROVIDING ALL LABOR, MATERIALS, TOOLS, TEST INSTRUMENTS, AND CONSUMABLES REQUIRED FOR THE INSTALLATION, TERMINATION, TESTING, LABELING, AND CERTIFICATION OF A FULLY FUNCTIONAL CATEGORY 6A OUTLET WITH THE PORT QUANTITY INDICATED.
- WHERE NEW DATA OUTLETS ARE BEING PROVIDED AND EXISTING DATA OUTLET CURRENTLY DOES NOT EXIST, PROVIDE (1) 1" CONDUIT FROM NEW BACKBOX TO ACCESSIBLE CEILING SPACE TO SECURELY ROUTE DATA CABLING FROM OUTLET TO TR VIA CABLE TRAY. IF CABLE TRAY IS NON-EXISTENT, EXTEND RACEWAY FROM OUTLET TO TR AS REQUIRED.
- PROVIDE CONDUITS AND SLEEVES AS REQUIRED FOR ROUTING AND INSTALLATION OF HORIZONTAL AND BACKBONE CABLING. PROVIDE FIRE-STOP MATERIALS TO SEAL IN AND AROUND CONDUIT PER CODE. REFER TO ARCHITECTURAL DRAWINGS FOR PARTITION TYPES AND WALL HEIGHTS.
- ALL TELECOMMUNICATION ROOMS SHALL BE PROVIDED WITH FIRE-RATED PLYWOOD BACKBOARDS. REFERENCE EXACT PLACEMENTS WITH ARCHITECTURE DRAWINGS AS REQUIRED.
- ANY LIVE SYSTEMS IN DEMO'D TR'S MUST REMAIN LIVE. CONTRACTOR TO COORDINATE WITH THE STATION TO IDENTIFY SYSTEMS THAT ARE LIVE. IF SYSTEMS ARE LIVE; INSTALL NEW CABLE FROM DEMO'D TR TO NEW TR. REFER TO DETAIL '3' ON TN506.
- RAIL KITS ARE PROVIDED BY THE GC FOR EQUIPMENT MOUNTED IN THE TR CHANNEL RACKS.
- LADDER RACK IN ALL TR'S WILL BE MOUNTED 6" OFF THE WALLS TO ACCOMMODATE ELECTRICAL AND MECHANICAL EQUIPMENT.

KEY NOTES

- EXISTING EQUIPMENT TO BE DEMOLISHED. ASSOCIATED RACEWAYS AND CABLING SHALL BE DEMOLISHED BACK TO SOURCE.
- EXISTING WIRELESS ACCESS POINT TO BE RE-FED WITH (2) CAT6A CABLES.
- PROVIDE RIGID CONDUIT SLEEVES WITH FIRE PROOFING AS REQUIRED. SIDE 'A' AND SIDE 'B' SLEEVES SHALL BE SEPARATED BY AT LEAST 10-FT.
- WIRE BASKET CABLE TRAY.
- PROVIDE (2)-DOOR ACCESS CONTROL PANEL TO SERVE ALL PACS DOOR SECURITY EQUIPMENT FOR THIS TR ROOM. PROVIDE ALL REQUIRED CONNECTIONS, PROGRAMMING, POWER SUPPLIES, AND COMPONENTS TO PROVIDE A COMPLETE AND FULLY FUNCTIONAL SYSTEM. REFERENCE SPECIFICATION "28 13 00 - PHYSICAL ACCESS CONTROL SYSTEM" FOR ADDITIONAL INFORMATION.

KEY PLAN

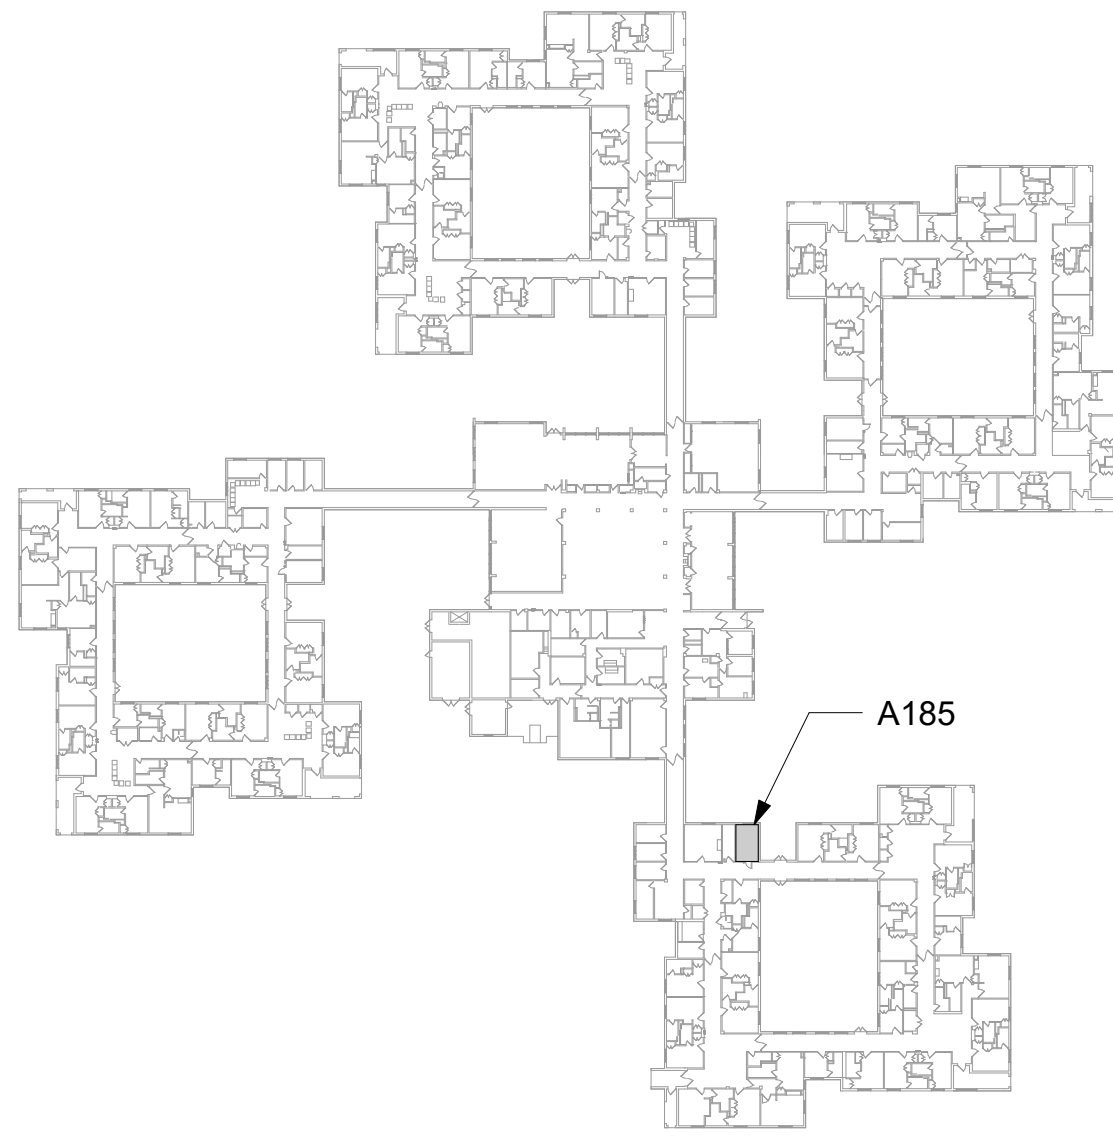


AREA SHOWN



1 RM A185 - DEMOLITION FLOOR PLAN

148TN101A 3/8" = 1'-0"

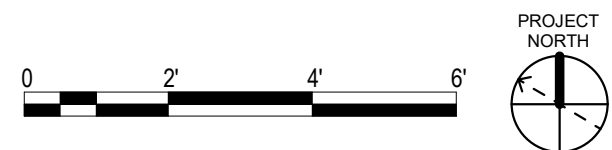


2 RM A185 - TELECOMMUNICATIONS PLAN

148TN101A 3/8" = 1'-0"



3 RM A185 - DEMOLITION OVERHEAD PLAN

148TN101A 3/8" = 1'-0"

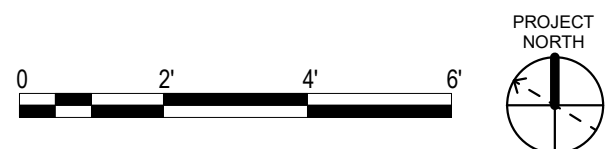

4 RM A185 - OVERHEAD PLAN


148TN101A 3/8" = 1'-0"



BM 360/599-22-700
Washington EHRMEE - BLDG
148-11
15/07/2025 11:10:30 am

VA FORM 08 - 6231


1 RM B185 - DEMOLITION FLOOR PLAN
148TN101A 1/2" = 1'-0"

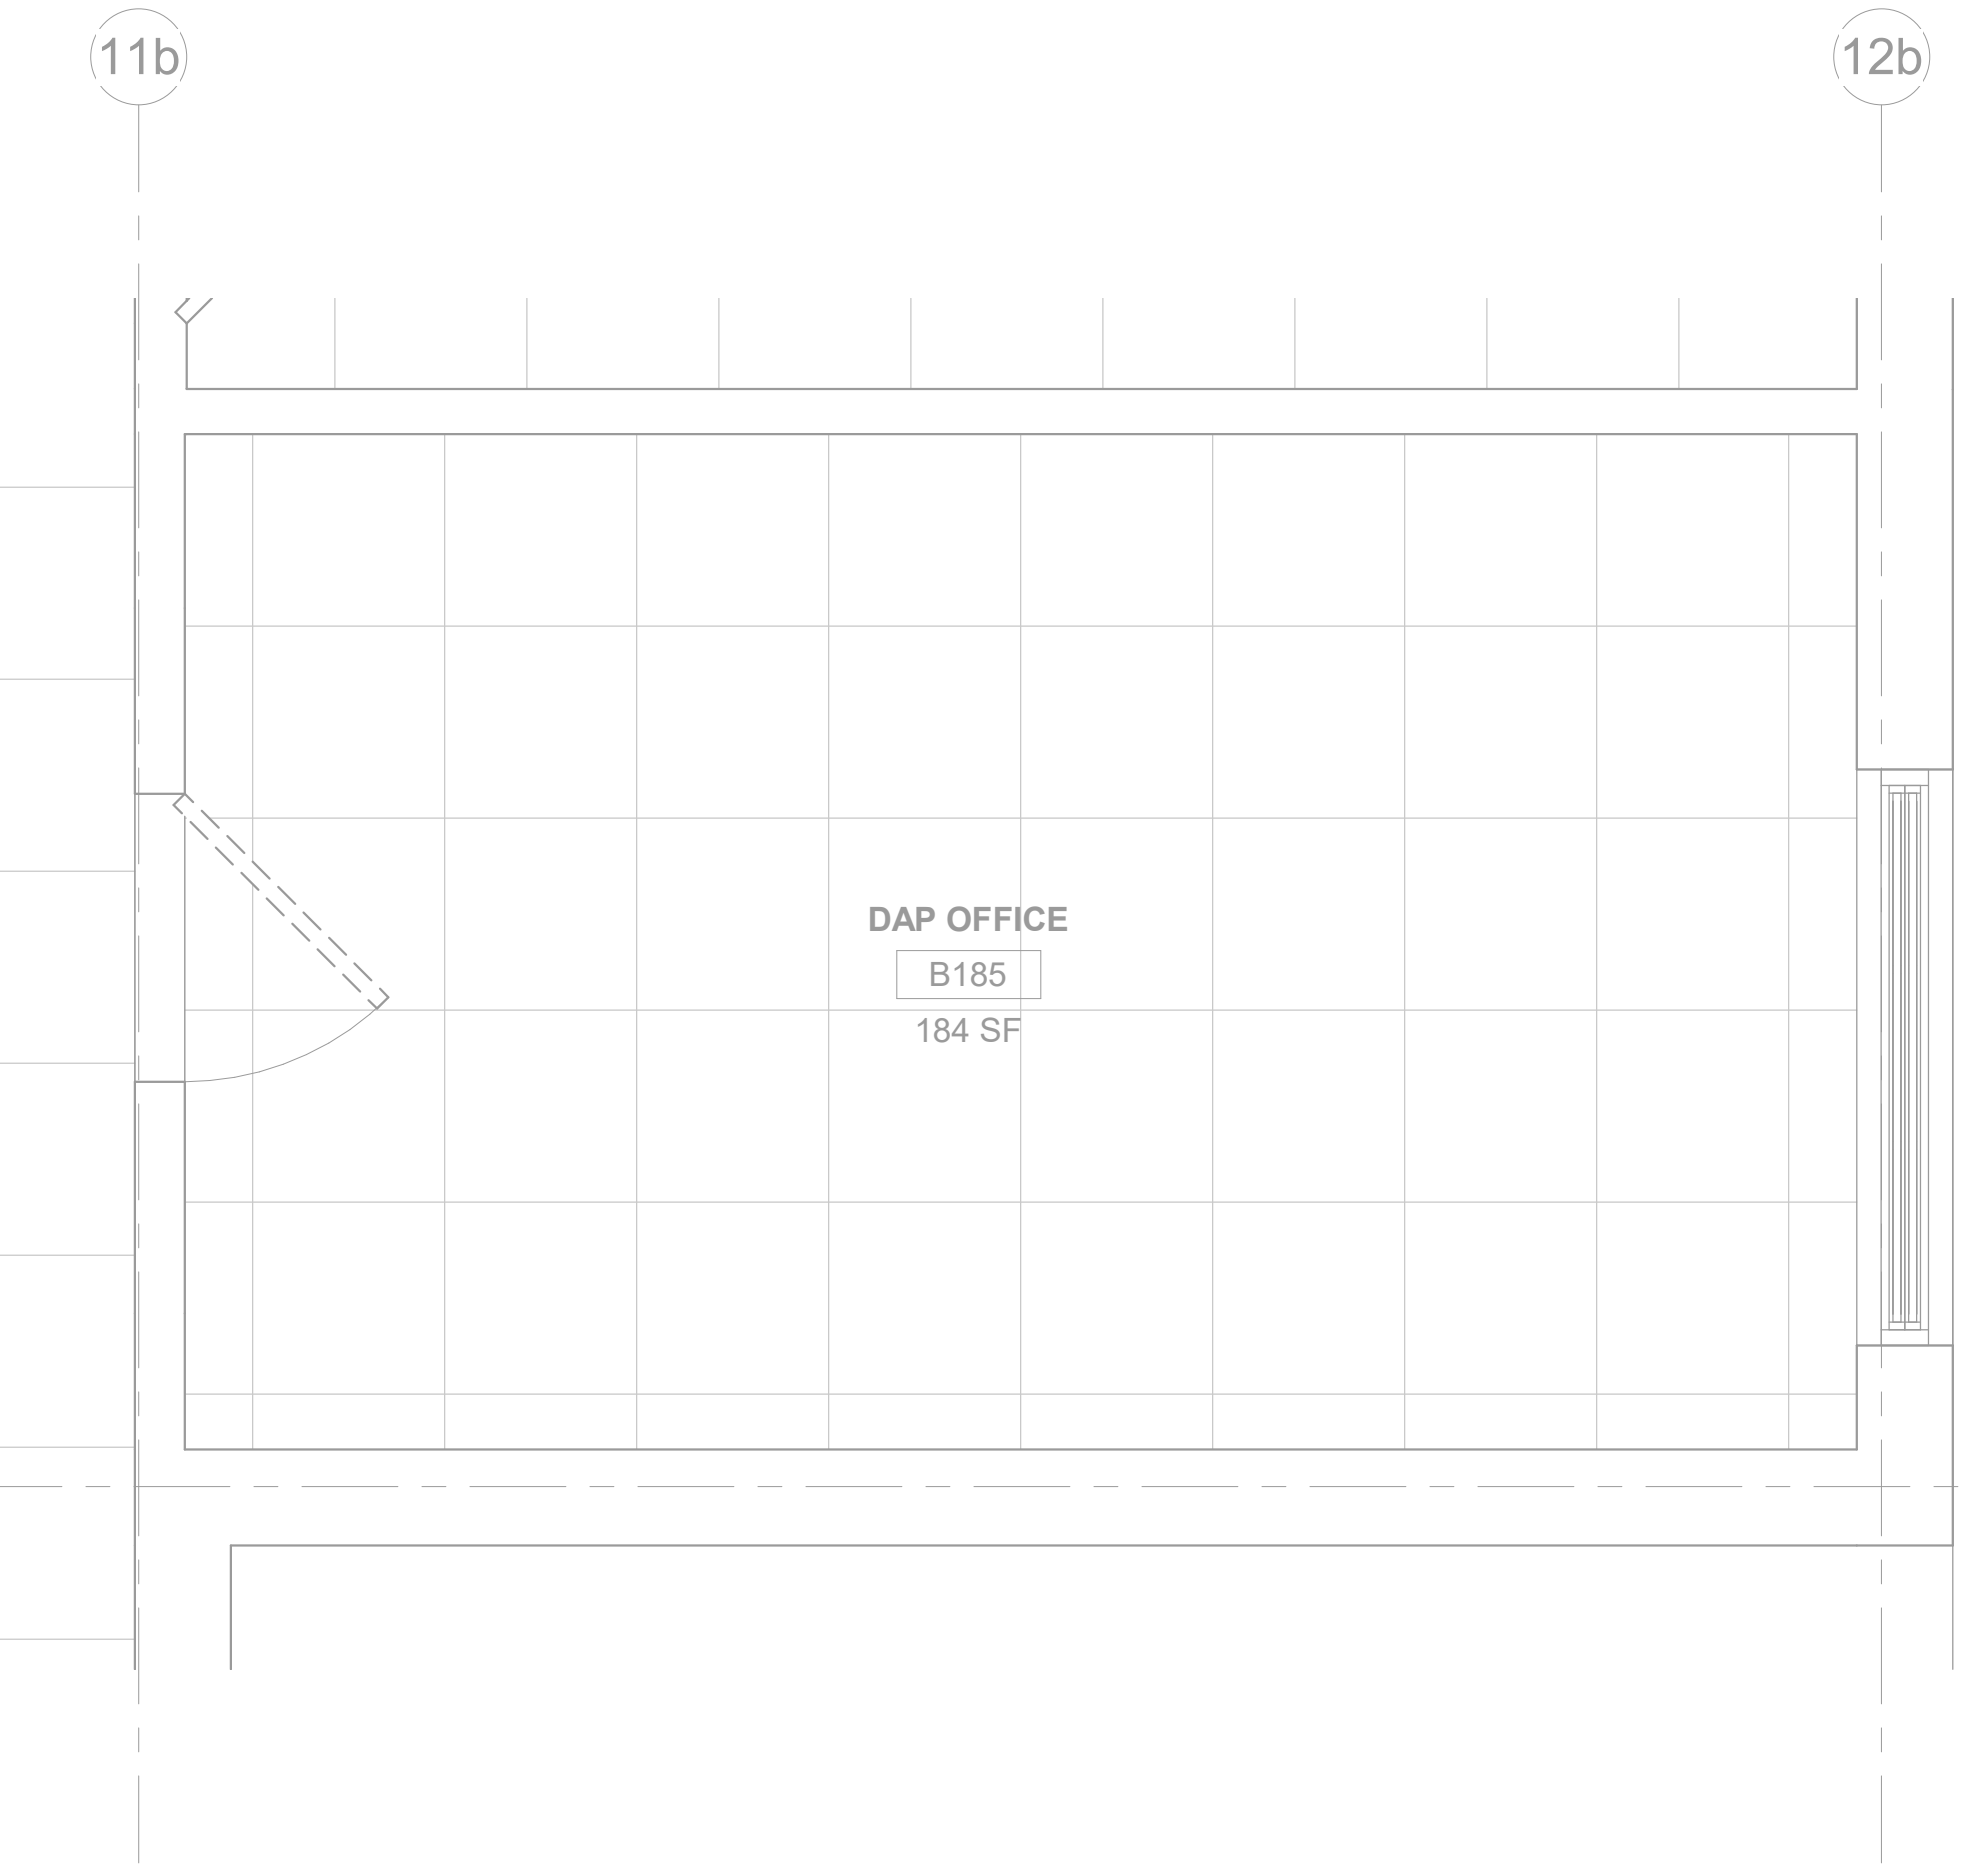


3 RM B185 - DEMOLITION OVERHEAD PLAN
148TN101A 1/2" = 1'-0"



2 RM B185 - TELECOMMUNICATIONS PLAN
148TN101A 1/2" = 1'-0"

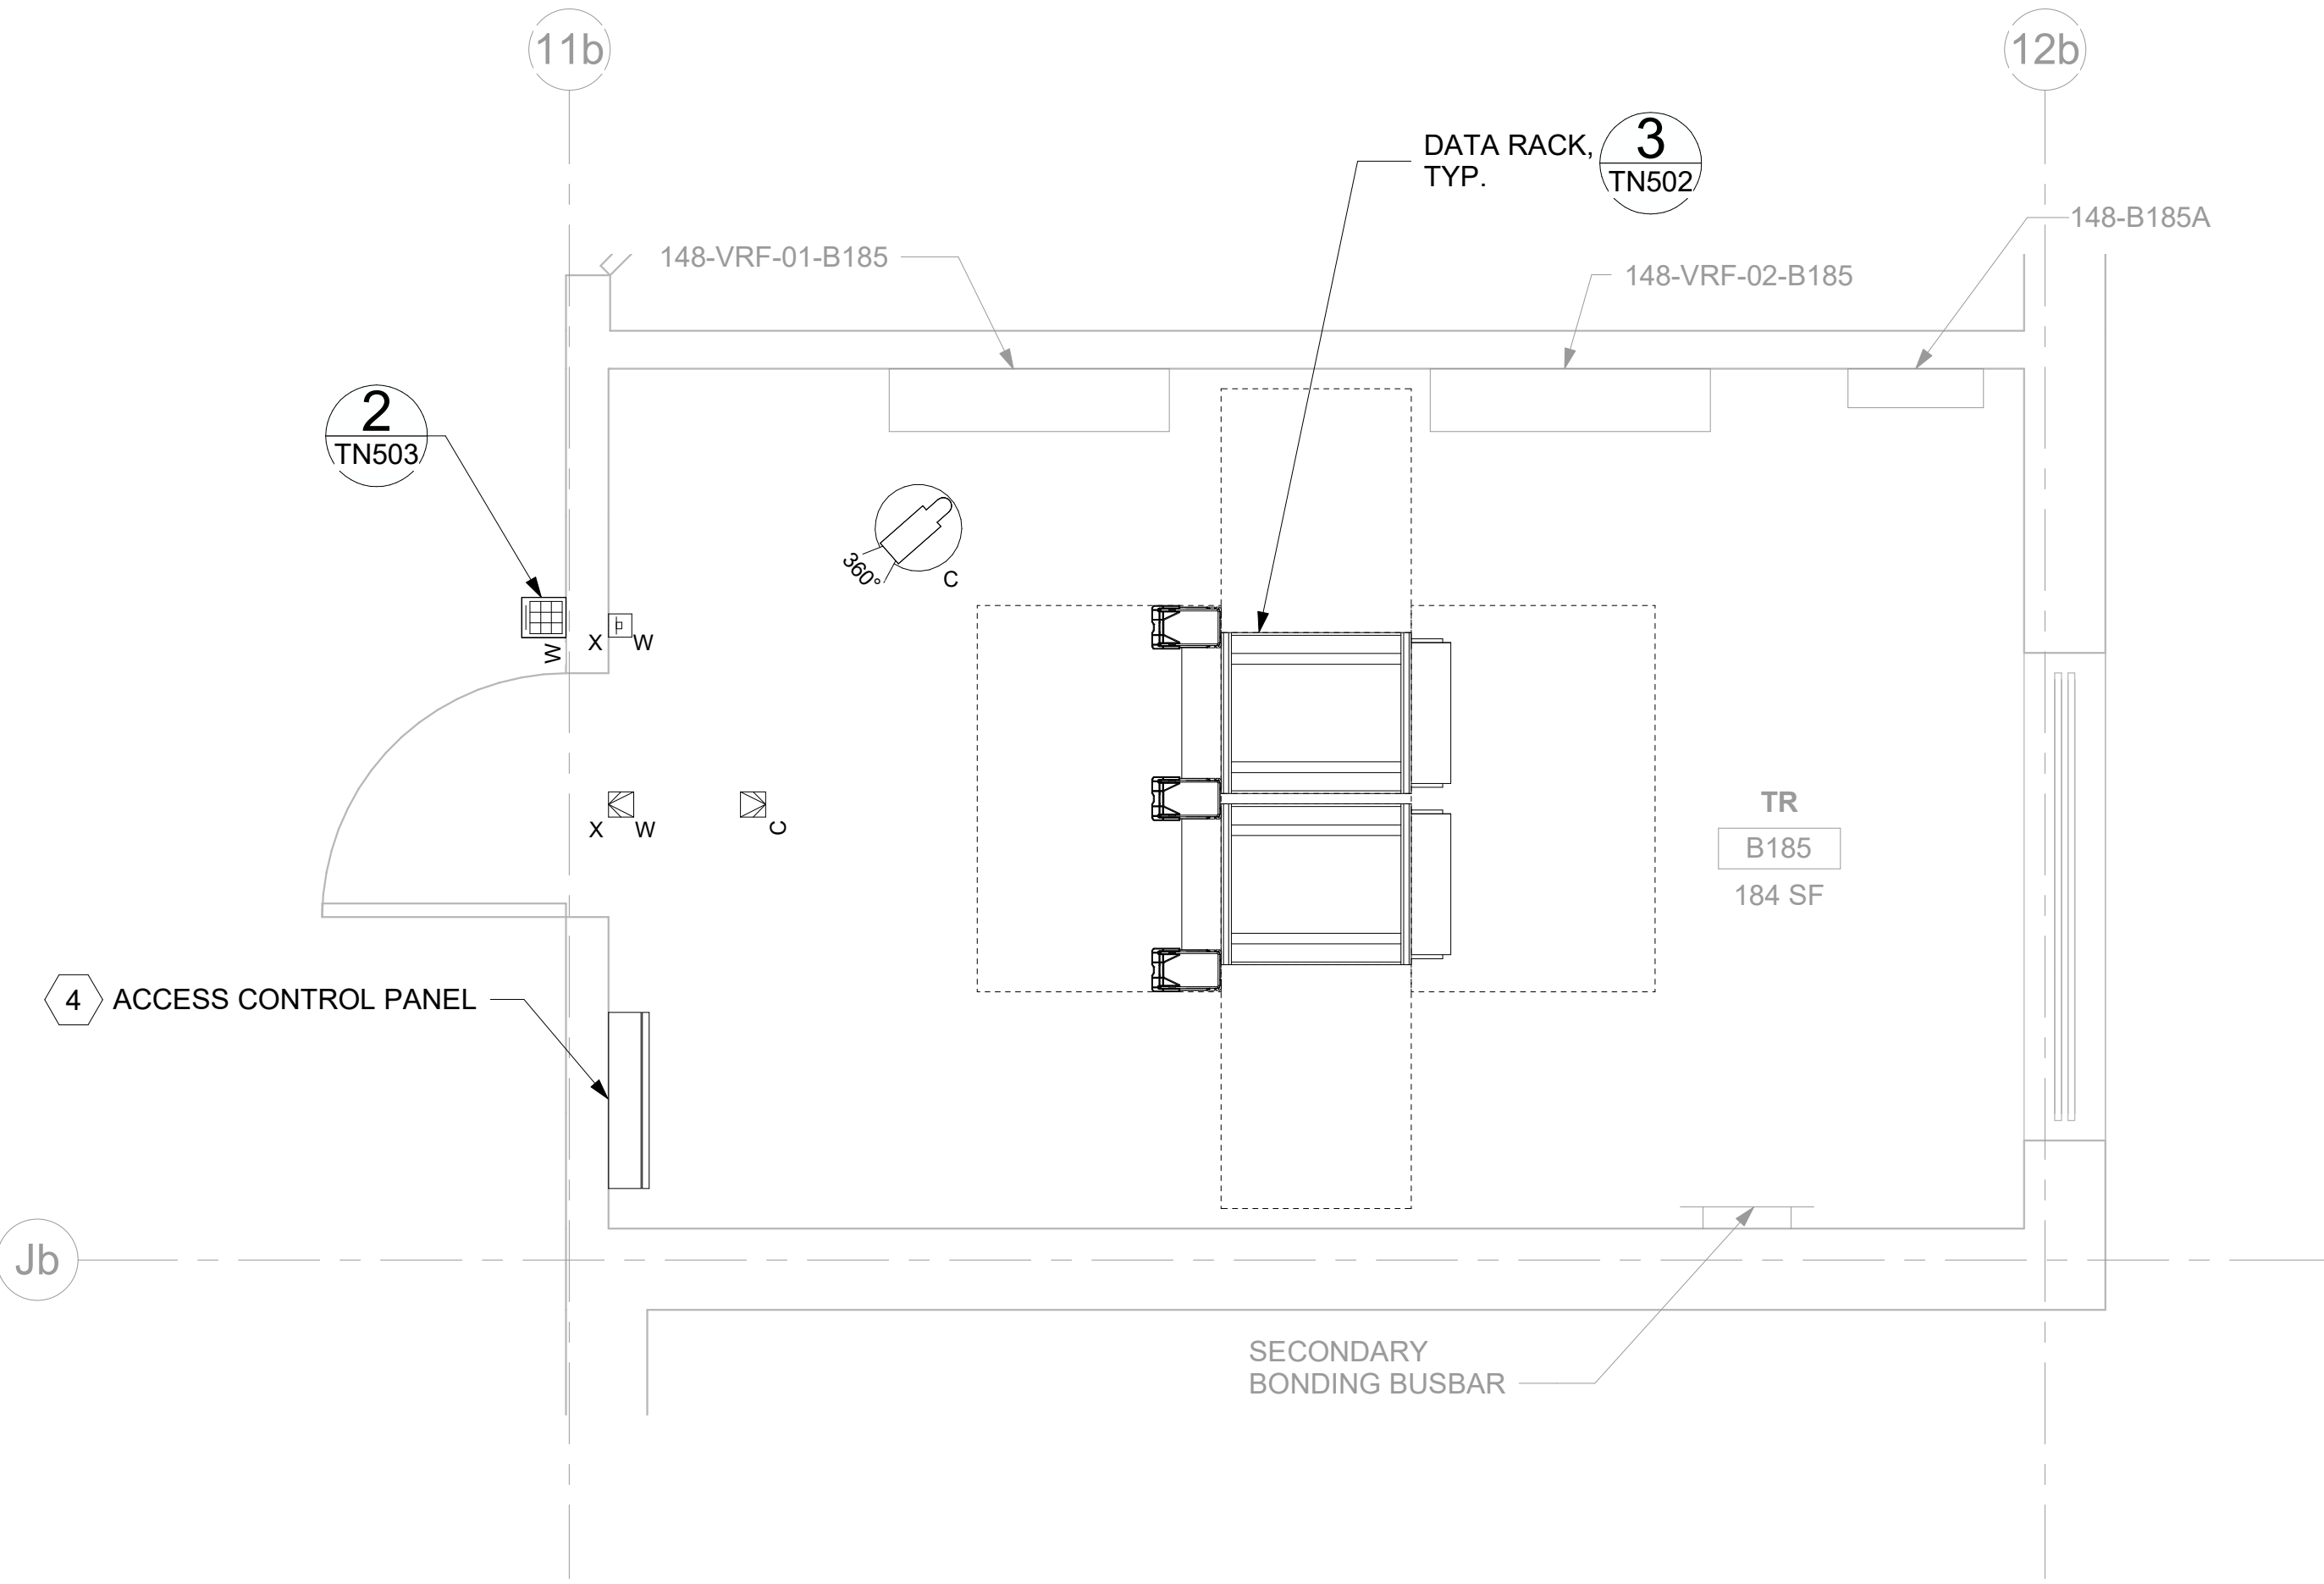

4 RM B185 - OVERHEAD PLAN
148TN101A 1/2" = 1'-0"

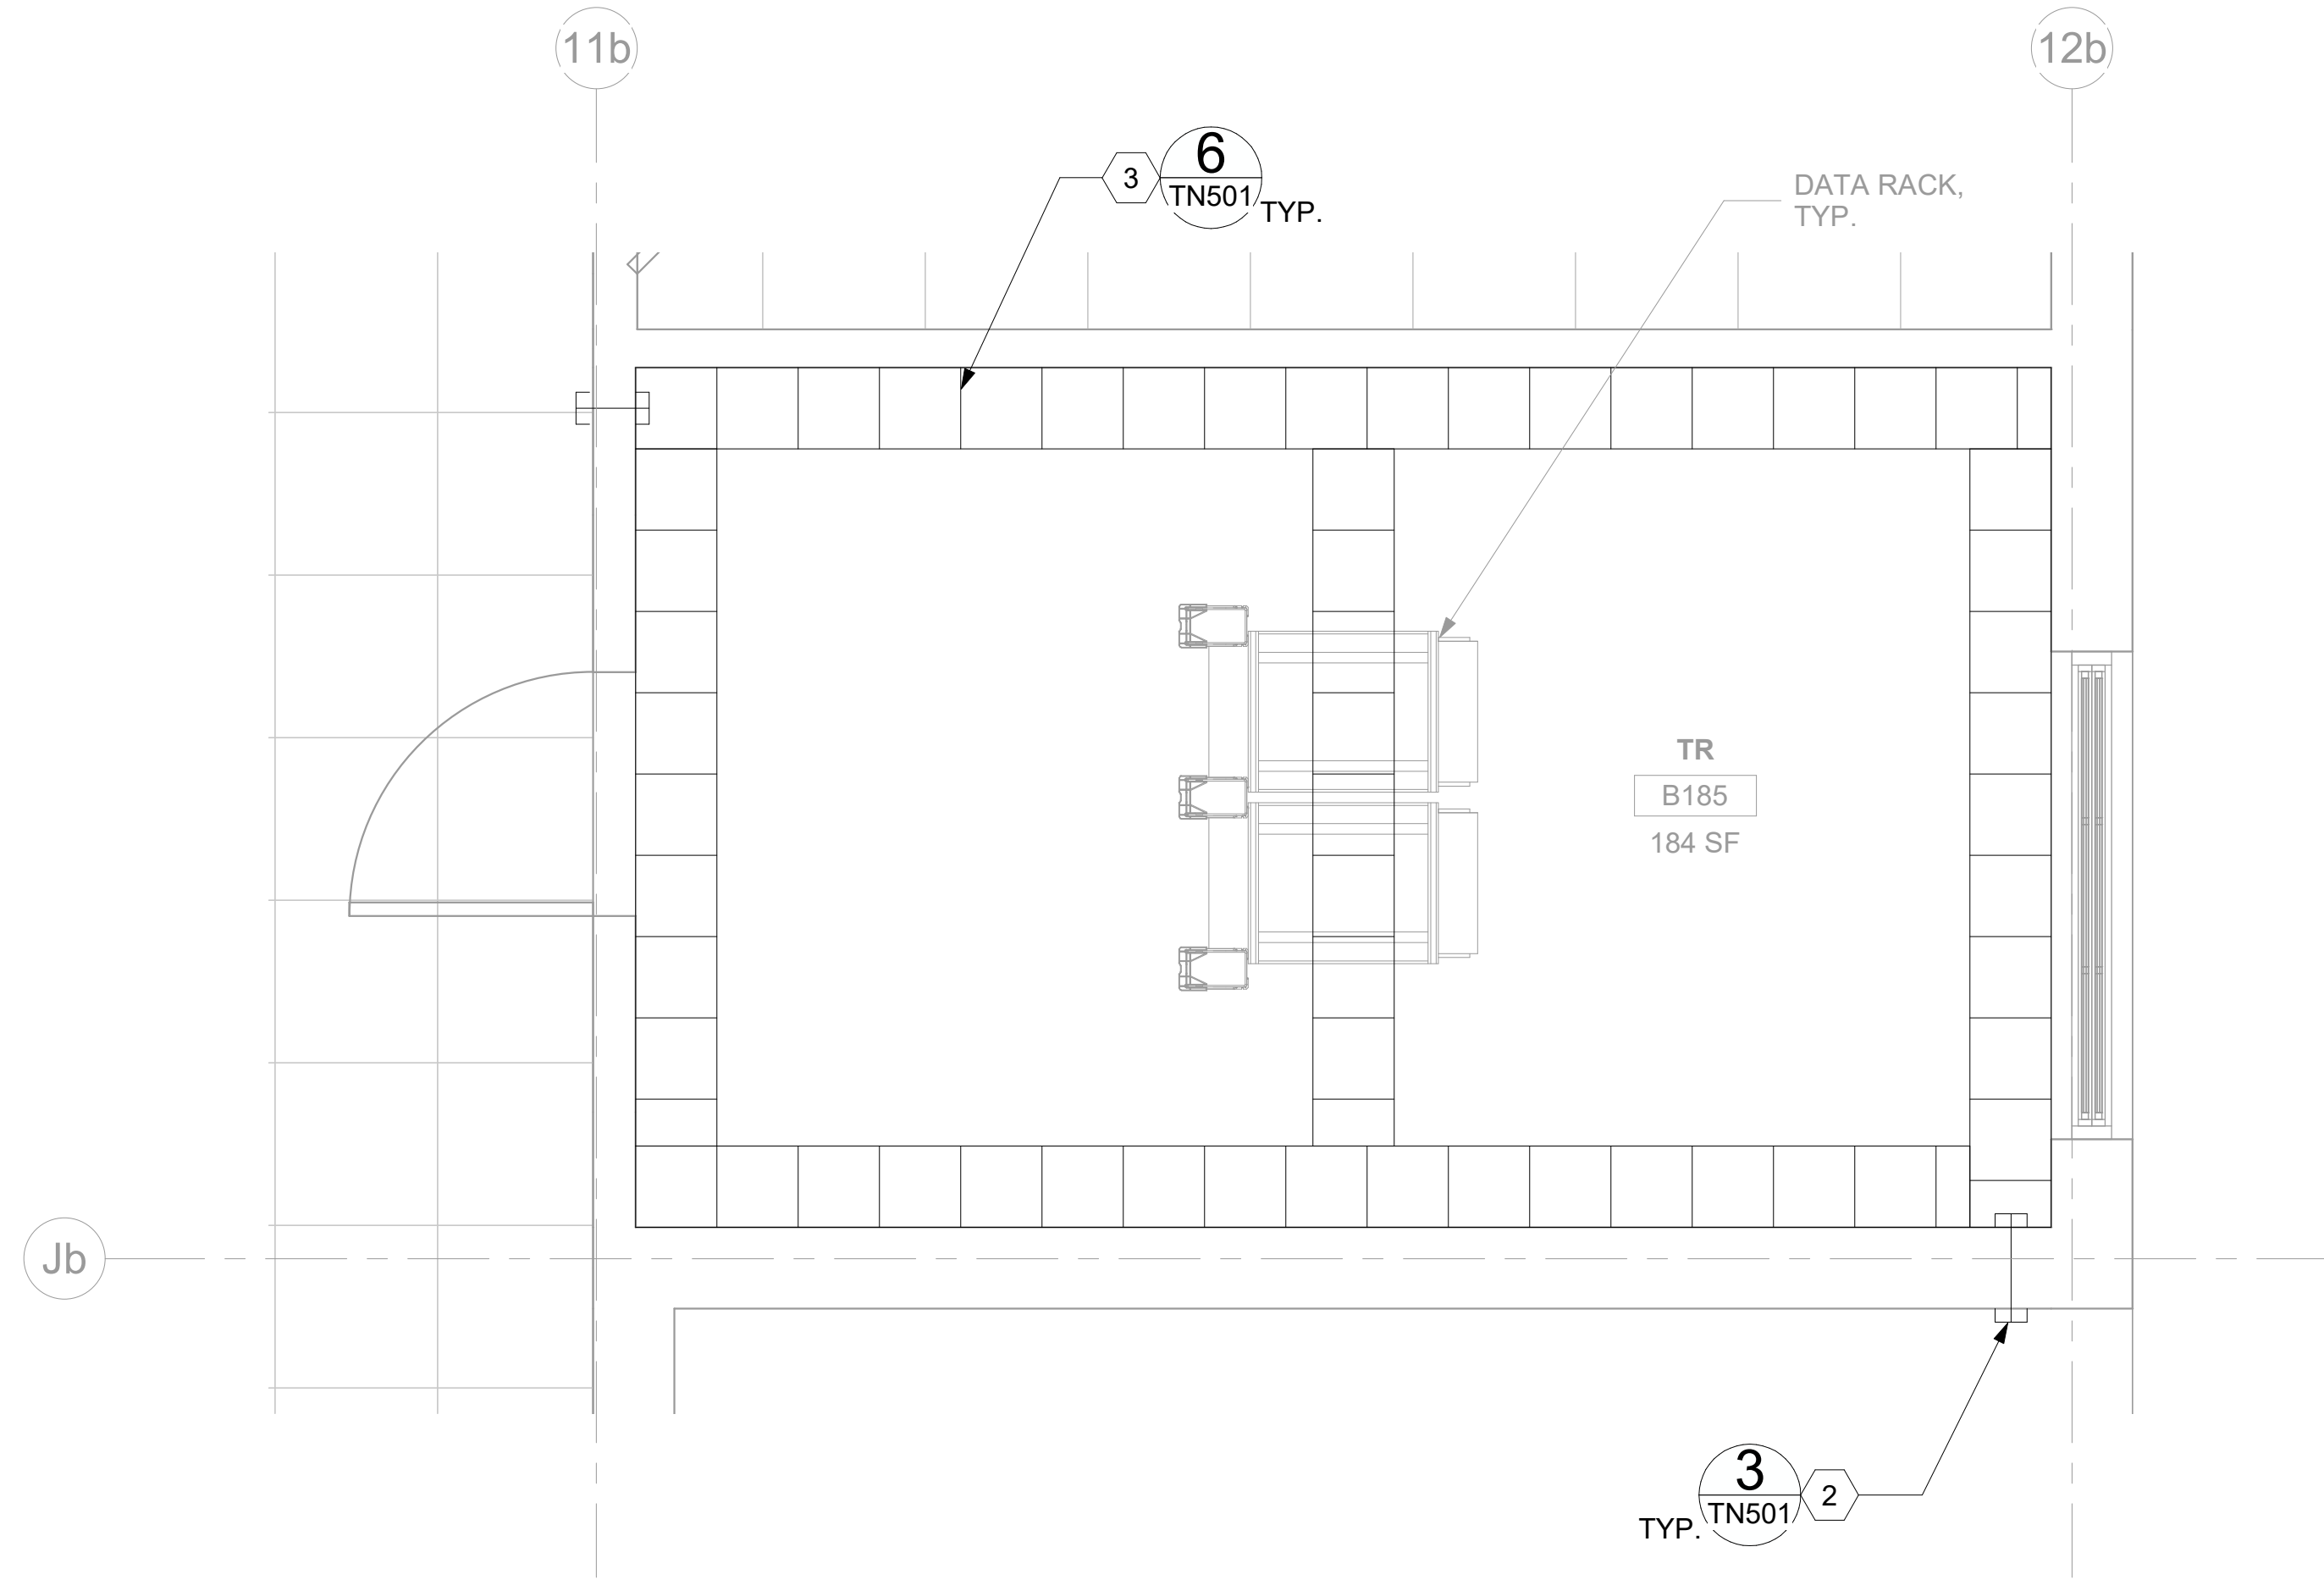


GENERAL NOTES

- PROTECT ALL EXISTING WORK FROM DAMAGE DURING CONSTRUCTION. ANY DAMAGED MATERIALS, SYSTEMS, COMPONENTS, FINISHES AND THE LIKE, SHALL BE REPAIRED OR REPLACED AT THE EXPENSE OF THE CONTRACTOR TO THE ACCEPTANCE OF THE OWNER.
- SEAL ALL INTERIOR WALL AND CEILING PENETRATIONS TO MATCH EXISTING FIRE RATING OR NEW FIRE RATING, IF REQUIRED. COORDINATE WITH ARCHITECTURAL DRAWINGS AS REQUIRED.
- ALL TELECOMMUNICATIONS CABLING CATEGORY 6 AND BELOW SHALL BE REMOVED AND REPLACED WITH CAT6A PORTS AND CABLE QUANTITIES INDICATED, UNLESS NOTED OTHERWISE.
- TELECOMMUNICATIONS CABLES SHALL BE ROUTED IN EXISTING PATHWAY VACATED BY EXISTING CABLING. PROVIDE RACEWAYS TO EXTEND TO ASSOCIATED TR.
- A TELECOMMUNICATIONS OUTLET UPGRADE SHALL INCLUDE, BUT IS NOT LIMITED TO REMOVING AND DISPOSING EXISTING DEVICES AND CABLES; PROVIDING ALL LABOR, MATERIALS, TOOLS, TEST INSTRUMENTS, AND CONSUMABLES REQUIRED FOR THE INSTALLATION, TERMINATION, TESTING, LABELING, AND CERTIFICATION OF A FULLY FUNCTIONAL CATEGORY 6A OUTLET WITH THE PORT QUANTITY INDICATED.
- WHERE NEW DATA OUTLETS ARE BEING PROVIDED AND EXISTING DATA OUTLET CURRENTLY DOES NOT EXIST, PROVIDE (1) 1" CONDUIT FROM NEW BACKBOX TO ACCESSIBLE CEILING SPACE TO SECURELY ROUTE DATA CABLING FROM OUTLET TO TR VIA CABLE TRAY. IF CABLE TRAY IS NON-EXISTENT, EXTEND RACEWAY FROM OUTLET TO TR AS REQUIRED.
- PROVIDE CONDUITS AND SLEEVES AS REQUIRED FOR ROUTING AND INSTALLATION OF HORIZONTAL AND BACKBONE CABLING. PROVIDE FIRE-STOP MATERIALS TO SEAL IN AND AROUND CONDUIT PER CODE. REFER TO ARCHITECTURAL DRAWINGS FOR PARTITION TYPES AND WALL HEIGHTS.
- ALL TELECOMMUNICATION ROOMS SHALL BE PROVIDED WITH FIRE-RATED PLYWOOD BACKBOARDS. REFERENCE EXACT PLACEMENTS WITH ARCHITECTURE DRAWINGS AS REQUIRED.
- ANY LIVE SYSTEMS IN DEMO'D TR'S MUST REMAIN LIVE. CONTRACTOR TO COORDINATE WITH THE STATION TO IDENTIFY SYSTEMS THAT ARE LIVE. IF SYSTEMS ARE LIVE; INSTALL NEW CABLE FROM DEMO'D TR TO NEW TR. REFER TO DETAIL '3' ON TN506.
- RAIL KITS ARE PROVIDED BY THE GC FOR EQUIPMENT MOUNTED IN THE TR CHANNEL RACKS.
- LADDER RACK IN ALL TR'S WILL BE MOUNTED 6" OFF THE WALLS TO ACCOMMODATE ELECTRICAL AND MECHANICAL EQUIPMENT.

KEY NOTES

- EXISTING EQUIPMENT TO BE DEMOLISHED. ASSOCIATED RACEWAYS AND CABLING SHALL BE DEMOLISHED BACK TO SOURCE.
- PROVIDE RIGID CONDUIT SLEEVES WITH FIRE PROOFING AS REQUIRED. SIDE 'A' AND SIDE 'B' SLEEVES SHALL BE SEPARATED BY AT LEAST 10-FT.
- WIRE BASKET CABLE TRAY.
- PROVIDE (2)-DOOR ACCESS CONTROL PANEL TO SERVE ALL PACS DOOR SECURITY EQUIPMENT FOR THIS TR ROOM. PROVIDE ALL REQUIRED CONNECTIONS, PROGRAMMING, POWER SUPPLIES, AND COMPONENTS TO PROVIDE A COMPLETE AND FULLY FUNCTIONAL SYSTEM. REFERENCE SPECIFICATION "28 13 00 - PHYSICAL ACCESS CONTROL SYSTEM" FOR ADDITIONAL INFORMATION.

KEY PLAN

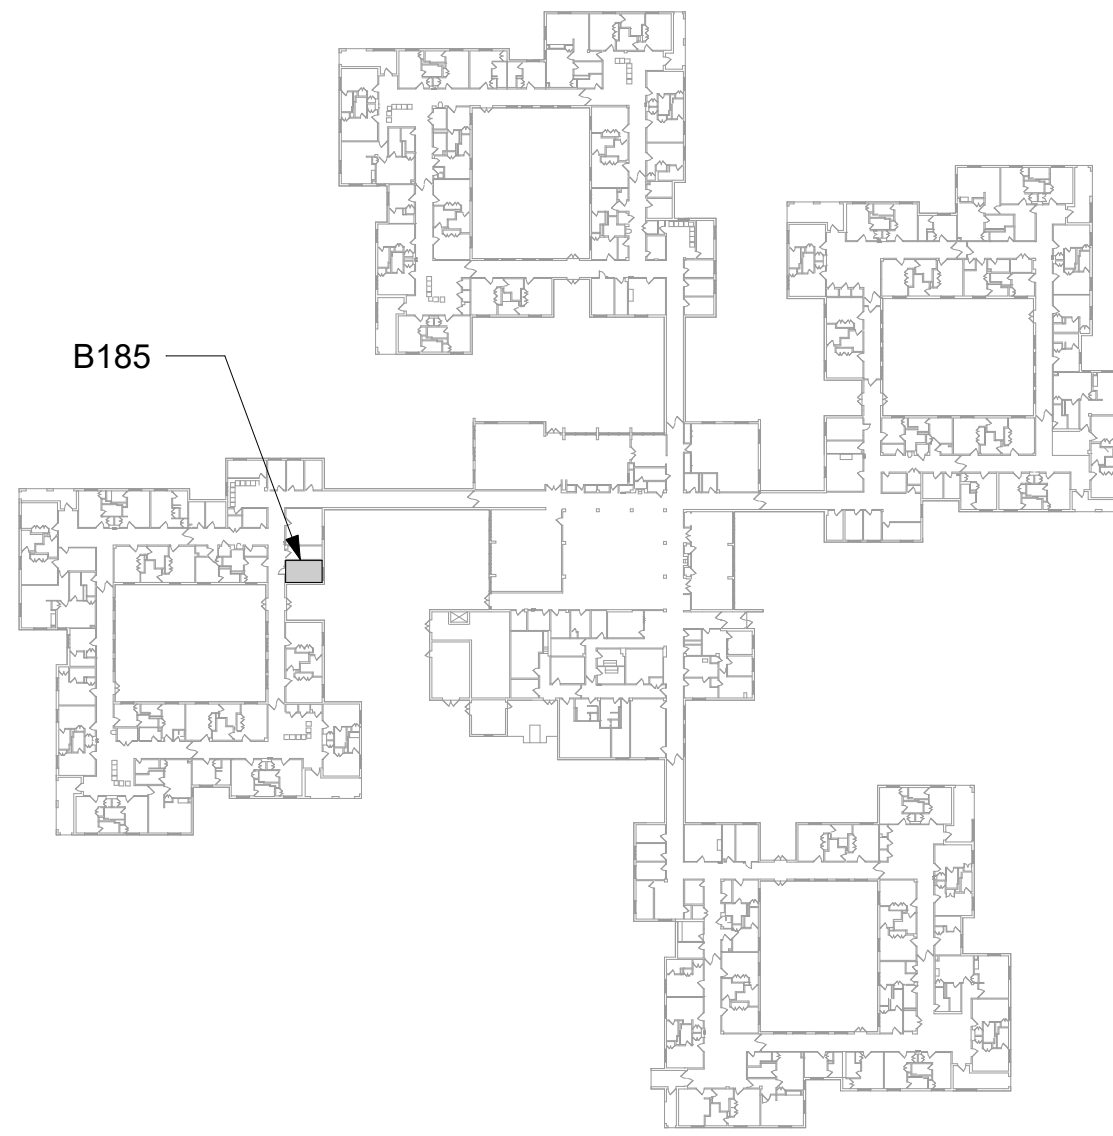

AREA SHOWN

CONSULTANT

ENGINEERING DISCIPLINE:

ARCHITECT/ENGINEER OF RECORD

A/E:
SPEES DESIGN BUILD
23830 PACIFIC HIGHWAY S. SUITE 203
KENT, WA 98032



STAMP



Office of
Construction
and Facilities
Management



U.S. Department
of Veterans Affairs

Drawing Title
BLDG 148 - LEVEL 01 - ENLARGED
TELECOMMUNICATIONS PLANS

Approved:

Phase
100% CONSTRUCTION
DOCUMENTS

FULLY SPRINKLERED

Project Title
EHRM INFRASTRUCTURE
UPGRADES - HAMPTON

Location
HAMPTON VA MEDICAL CENTER, HAMPTON, VIRGINIA

Issue Date
07/18/2025

Checked
KG

Drawn
BCL/GPB

Project Number
590-22-700
Building Number
148

Drawing Number
148TN401b
606 of 713

BM 360/599-22-700
Washington EHRMEE - BLDG
148-11
15/07/2025 11:10:41 am

VA FORM 08 - 6231

CONSULTANT

ENGINEERING DISCIPLINE:

ARCHITECT/ENGINEER OF RECORD

A/E:
SPEES DESIGN BUILD
23830 PACIFIC HIGHWAY S. SUITE 203
KENT, WA 98032



STAMP



Office of
Construction
and Facilities
Management



U.S. Department
of Veterans Affairs

Drawing Title

BLDG 148 - LEVEL 01 - ENLARGED
TELECOMMUNICATIONS PLANS

Approved:

Phase

100% CONSTRUCTION
DOCUMENTS

Project Title

EHRM INFRASTRUCTURE
UPGRADES - HAMPTON

Project Number

590-22-700

Building Number

148

Drawing Number

148TN401c

607 of 713


GENERAL NOTES

- PROTECT ALL EXISTING WORK FROM DAMAGE DURING CONSTRUCTION. ANY DAMAGED MATERIALS, SYSTEMS, COMPONENTS, FINISHES AND THE LIKE, SHALL BE REPAIRED OR REPLACED AT THE EXPENSE OF THE CONTRACTOR TO THE ACCEPTANCE OF THE OWNER.
- SEAL ALL INTERIOR WALL AND CEILING PENETRATIONS TO MATCH EXISTING FIRE RATING OR NEW FIRE RATING, IF REQUIRED. COORDINATE WITH ARCHITECTURAL DRAWINGS AS REQUIRED.
- ALL TELECOMMUNICATIONS CABLING CATEGORY 6 AND BELOW SHALL BE REMOVED AND REPLACED WITH CAT6A PORTS AND CABLE QUANTITIES INDICATED, UNLESS NOTED OTHERWISE.
- TELECOMMUNICATIONS CABLES SHALL BE ROUTED IN EXISTING PATHWAY VACATED BY EXISTING CABLING. PROVIDE RACEWAYS TO EXTEND TO ASSOCIATED TR.
- A TELECOMMUNICATIONS OUTLET UPGRADE SHALL INCLUDE, BUT IS NOT LIMITED TO REMOVING AND DISPOSING EXISTING DEVICES AND CABLES; PROVIDING ALL LABOR, MATERIALS, TOOLS, TEST INSTRUMENTS, AND CONSUMABLES REQUIRED FOR THE INSTALLATION, TERMINATION, TESTING, LABELING, AND CERTIFICATION OF A FULLY FUNCTIONAL CATEGORY 6A OUTLET WITH THE PORT QUANTITY INDICATED.
- WHERE NEW DATA OUTLETS ARE BEING PROVIDED AND EXISTING DATA OUTLET CURRENTLY DOES NOT EXIST, PROVIDE (1) 1" CONDUIT FROM NEW BACKBOX TO ACCESSIBLE CEILING SPACE TO SECURELY ROUTE DATA CABLING FROM OUTLET TO TR VIA CABLE TRAY. IF CABLE TRAY IS NON-EXISTENT, EXTEND RACEWAY FROM OUTLET TO TR AS REQUIRED.
- PROVIDE CONDUITS AND SLEEVES AS REQUIRED FOR ROUTING AND INSTALLATION OF HORIZONTAL AND BACKBONE CABLING. PROVIDE FIRE-STOP MATERIALS TO SEAL IN AND AROUND CONDUIT PER CODE. REFER TO ARCHITECTURAL DRAWINGS FOR PARTITION TYPES AND WALL HEIGHTS.
- ALL TELECOMMUNICATION ROOMS SHALL BE PROVIDED WITH FIRE-RATED PLYWOOD BACKBOARDS. REFERENCE EXACT PLACEMENTS WITH ARCHITECTURE DRAWINGS AS REQUIRED.
- ANY LIVE SYSTEMS IN DEMO'D TR'S MUST REMAIN LIVE. CONTRACTOR TO COORDINATE WITH THE STATION TO IDENTIFY SYSTEMS THAT ARE LIVE. IF SYSTEMS ARE LIVE, INSTALL NEW CABLE FROM DEMO'D TR TO NEW TR. REFER TO DETAIL '3' ON TN506.
- RAIL KITS ARE PROVIDED BY THE GC FOR EQUIPMENT MOUNTED IN THE TR CHANNEL RACKS.
- LADDER RACK IN ALL TR'S WILL BE MOUNTED 6" OFF THE WALLS TO ACCOMMODATE ELECTRICAL AND MECHANICAL EQUIPMENT.

KEY NOTES

- EXISTING EQUIPMENT TO BE DEMOLISHED. ASSOCIATED RACEWAYS AND CABLING SHALL BE DEMOLISHED BACK TO SOURCE.
- PROVIDE RIGID CONDUIT SLEEVES WITH FIRE PROOFING AS REQUIRED. SIDE 'A' AND SIDE 'B' SLEEVES SHALL BE SEPARATED BY AT LEAST 10-FT.
- WIRE BASKET CABLE TRAY.
- PROVIDE (2)-DOOR ACCESS CONTROL PANEL TO SERVE ALL PACS DOOR SECURITY EQUIPMENT FOR THIS TR ROOM. PROVIDE ALL REQUIRED CONNECTIONS, PROGRAMMING, POWER SUPPLIES, AND COMPONENTS TO PROVIDE A COMPLETE AND FULLY FUNCTIONAL SYSTEM. REFERENCE SPECIFICATION "28 13 00 - PHYSICAL ACCESS CONTROL SYSTEM" FOR ADDITIONAL INFORMATION.
- EXISTING WIRELESS ACCESS POINT TO BE RE-FED WITH (2) CAT6A CABLES.

KEY PLAN

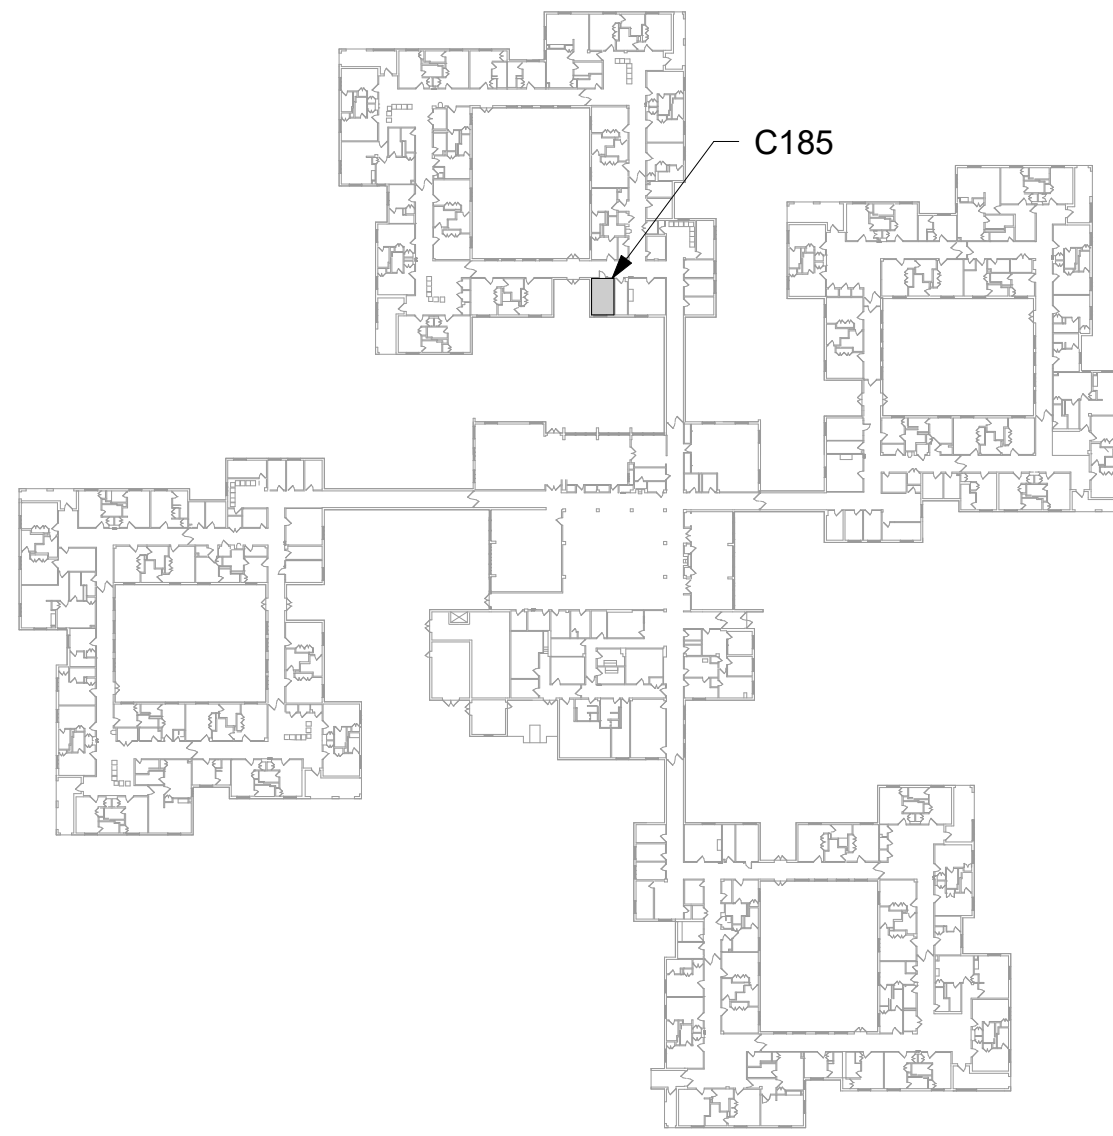


AREA SHOWN




1 RM C185 - DEMOLITION FLOOR PLAN

148TN101A 1/2" = 1'-0"

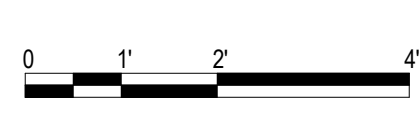


2 RM C185 - TELECOMMUINCATIONS PLAN

148TN101A 1/2" = 1'-0"

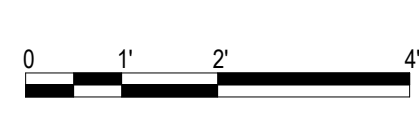


3 RM C185 - DEMOLITION OVERHEAD PLAN

148TN101A 1/2" = 1'-0"

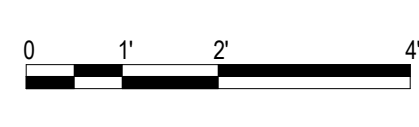

4 RM C185 - OVERHEAD PLAN

148TN101A 1/2" = 1'-0"

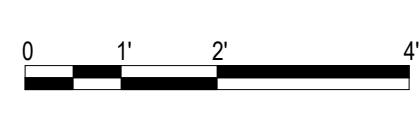

BM 360/599-22-700
Washington EHRMEE - BLDG
148-11
7/15/2025 12:10:29 PM

VA FORM 08 - 6231

CONSULTANT

ENGINEERING DISCIPLINE:

ARCHITECT/ENGINEER OF RECORD

A/E:
SPEES DESIGN BUILD
23830 PACIFIC HIGHWAY S. SUITE 203
KENT, WA 98032



STAMP



Office of
Construction
and Facilities
Management



U.S. Department
of Veterans Affairs

Drawing Title

BLDG 148 - LEVEL 01 - ENLARGED
TELECOMMUNICATIONS PLANS

Approved:

Phase

100% CONSTRUCTION
DOCUMENTS

FULLY SPRINKLERED

Project Title

EHRM INFRASTRUCTURE
UPGRADES - HAMPTON

Location

HAMPTON VA MEDICAL CENTER, HAMPTON, VIRGINIA

Issue Date

07/18/2025

Checked

KG

Drawn

BCL/GPB

Project Number

590-22-700

Building Number

148

Drawing Number

148TN401d

608 of 713


GENERAL NOTES

- PROTECT ALL EXISTING WORK FROM DAMAGE DURING CONSTRUCTION. ANY DAMAGED MATERIALS, SYSTEMS, COMPONENTS, FINISHES AND THE LIKE, SHALL BE REPAIRED OR REPLACED AT THE EXPENSE OF THE CONTRACTOR TO THE ACCEPTANCE OF THE OWNER.
- SEAL ALL INTERIOR WALL AND CEILING PENETRATIONS TO MATCH EXISTING FIRE RATING OR NEW FIRE RATING, IF REQUIRED. COORDINATE WITH ARCHITECTURAL DRAWINGS AS REQUIRED.
- ALL TELECOMMUNICATIONS CABLING CATEGORY 6 AND BELOW SHALL BE REMOVED AND REPLACED WITH CAT6A PORTS AND CABLE QUANTITIES INDICATED, UNLESS NOTED OTHERWISE.
- TELECOMMUNICATIONS CABLES SHALL BE ROUTED IN EXISTING PATHWAY VACATED BY EXISTING CABLING. PROVIDE RACEWAYS TO EXTEND TO ASSOCIATED TR.
- A TELECOMMUNICATIONS OUTLET UPGRADE SHALL INCLUDE, BUT IS NOT LIMITED TO REMOVING AND DISPOSING EXISTING DEVICES AND CABLES; PROVIDING ALL LABOR, MATERIALS, TOOLS, TEST INSTRUMENTS, AND CONSUMABLES REQUIRED FOR THE INSTALLATION, TERMINATION, TESTING, LABELING, AND CERTIFICATION OF A FULLY FUNCTIONAL CATEGORY 6A OUTLET WITH THE PORT QUANTITY INDICATED.
- WHERE NEW DATA OUTLETS ARE BEING PROVIDED AND EXISTING DATA OUTLET CURRENTLY DOES NOT EXIST, PROVIDE (1) 1" CONDUIT FROM NEW BACKBOX TO ACCESSIBLE CEILING SPACE TO SECURELY ROUTE DATA CABLING FROM OUTLET TO TR VIA CABLE TRAY. IF CABLE TRAY IS NON-EXISTENT, EXTEND RACEWAY FROM OUTLET TO TR AS REQUIRED.
- PROVIDE CONDUITS AND SLEEVES AS REQUIRED FOR ROUTING AND INSTALLATION OF HORIZONTAL AND BACKBONE CABLING. PROVIDE FIRE-STOP MATERIALS TO SEAL IN AND AROUND CONDUIT PER CODE. REFER TO ARCHITECTURAL DRAWINGS FOR PARTITION TYPES AND WALL HEIGHTS.
- ALL TELECOMMUNICATION ROOMS SHALL BE PROVIDED WITH FIRE-RATED PLYWOOD BACKBOARDS. REFERENCE EXACT PLACEMENTS WITH ARCHITECTURE DRAWINGS AS REQUIRED.
- ANY LIVE SYSTEMS IN DEMO'D TR'S MUST REMAIN LIVE. CONTRACTOR TO COORDINATE WITH THE STATION TO IDENTIFY SYSTEMS THAT ARE LIVE. IF SYSTEMS ARE LIVE; INSTALL NEW CABLE FROM DEMO'D TR TO NEW TR. REFER TO DETAIL '3' ON TN506.
- RAIL KITS ARE PROVIDED BY THE GC FOR EQUIPMENT MOUNTED IN THE TR CHANNEL RACKS.
- LADDER RACK IN ALL TR'S WILL BE MOUNTED 6" OFF THE WALLS TO ACCOMMODATE ELECTRICAL AND MECHANICAL EQUIPMENT.


KEY NOTES

- PROVIDE RIGID CONDUIT SLEEVES WITH FIRE PROOFING AS REQUIRED. SIDE 'A' AND SIDE 'B' SLEEVES SHALL BE SEPARATED BY AT LEAST 10'-FT.
- WIRE BASKET CABLE TRAY.

KEY PLAN


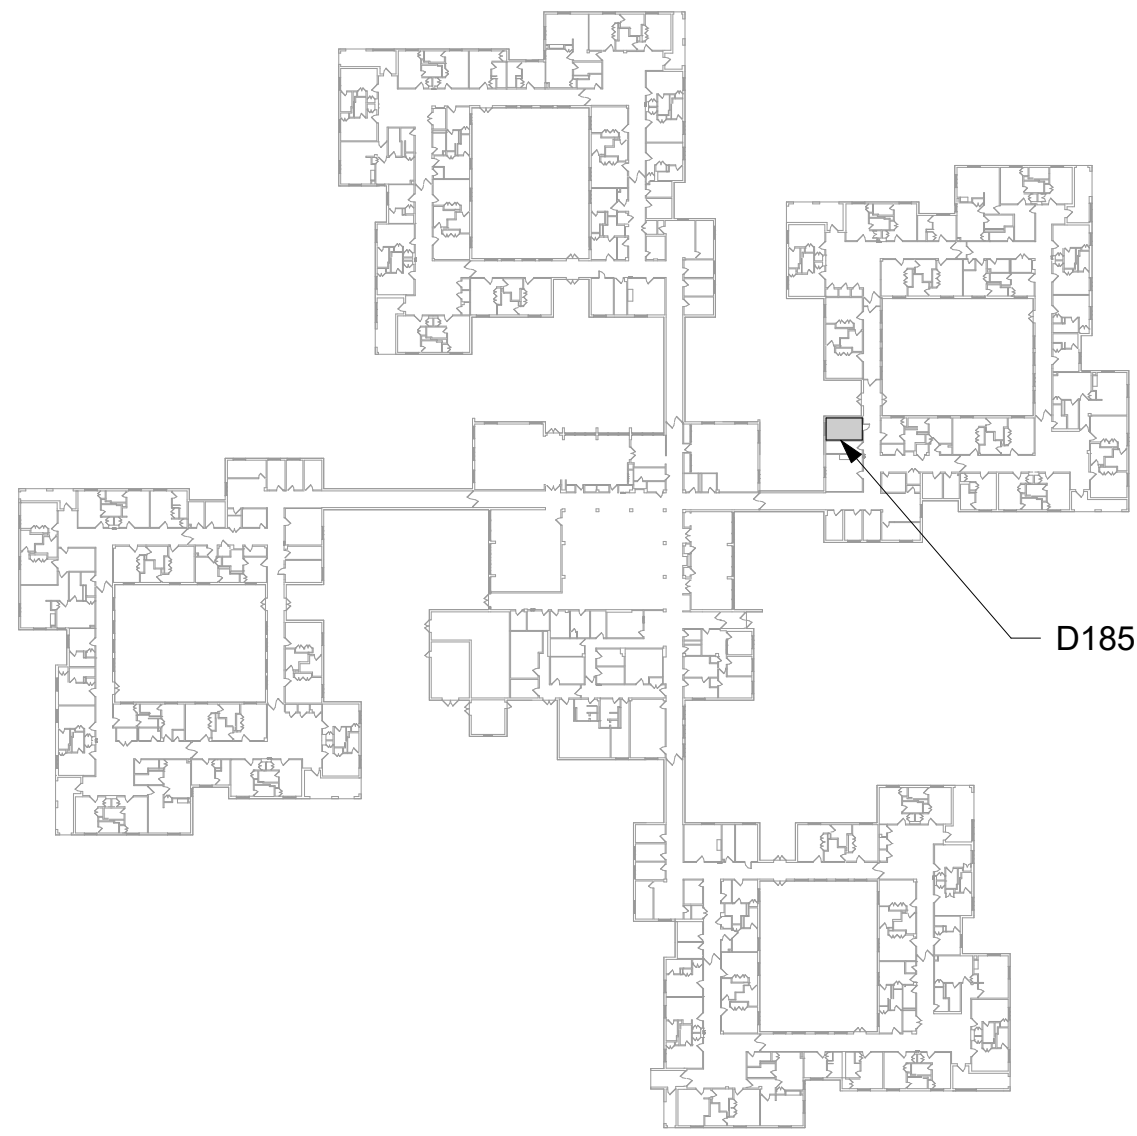


AREA SHOWN

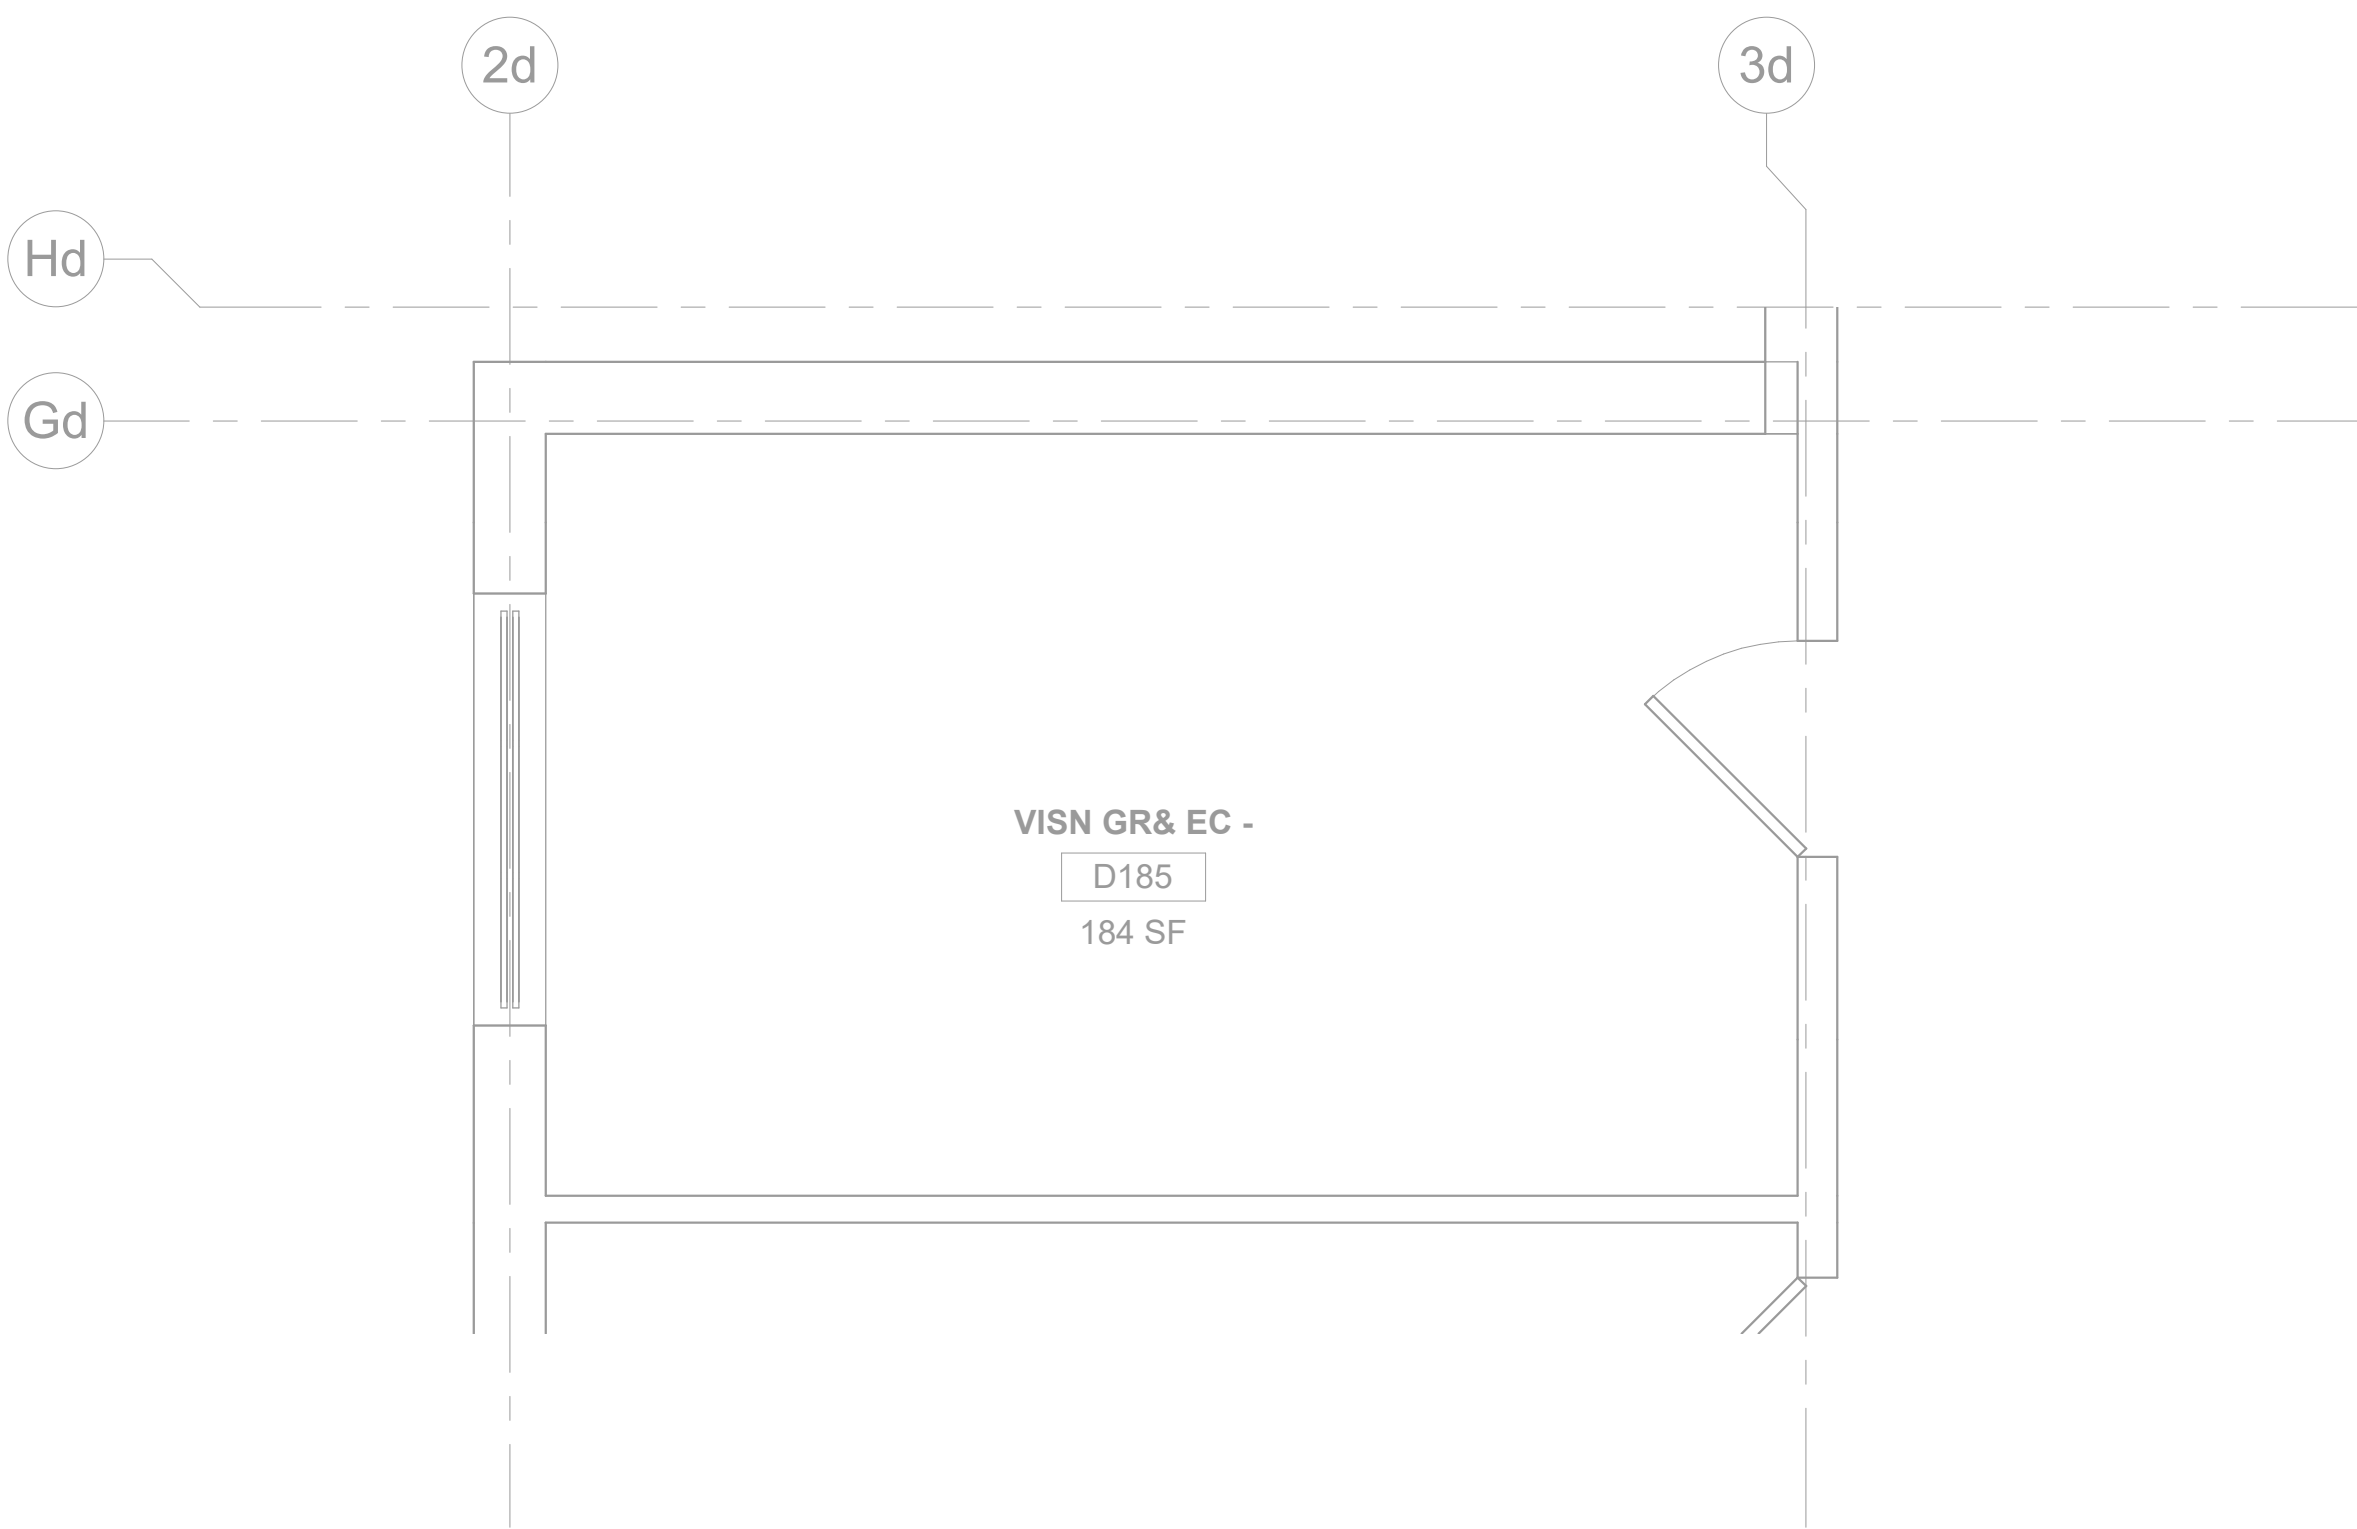


1 RM D185 - DEMOLITION FLOOR PLAN

148TN101B 1" = 25'-0"

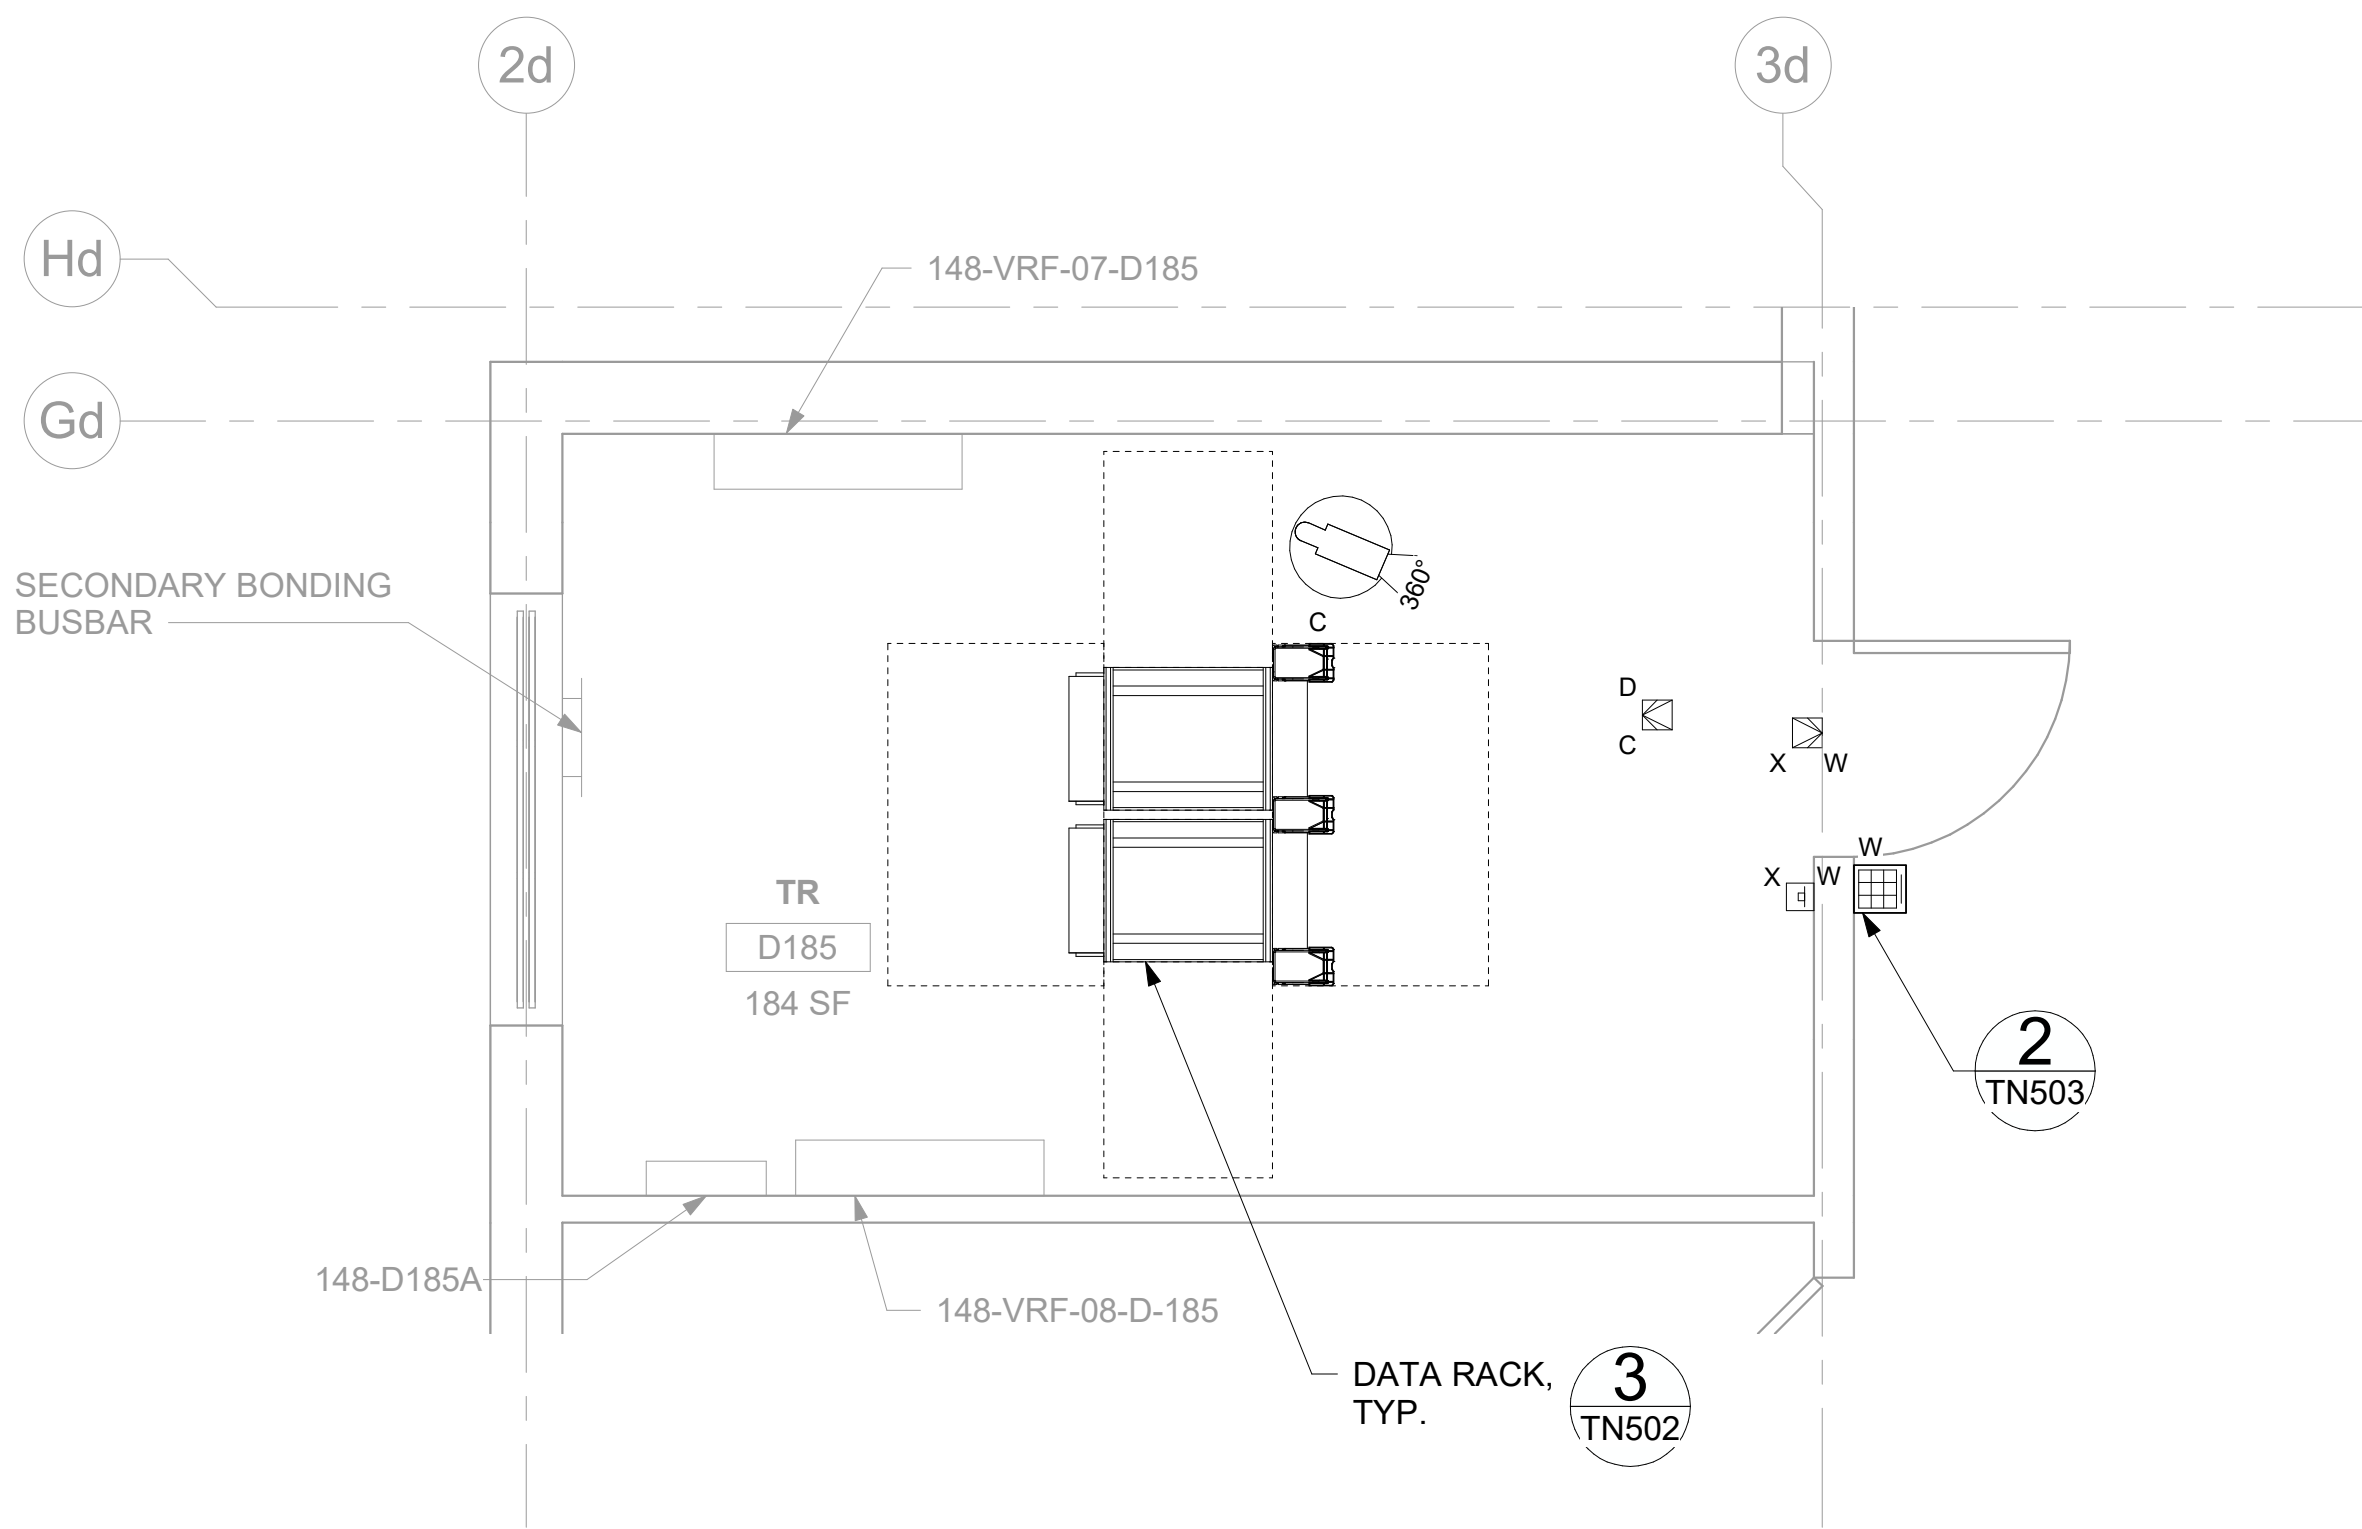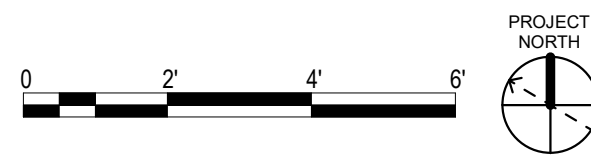



2 RM D185 - TELECOMMUNICATIONS PLAN

148TN101B 1" = 25'-0"

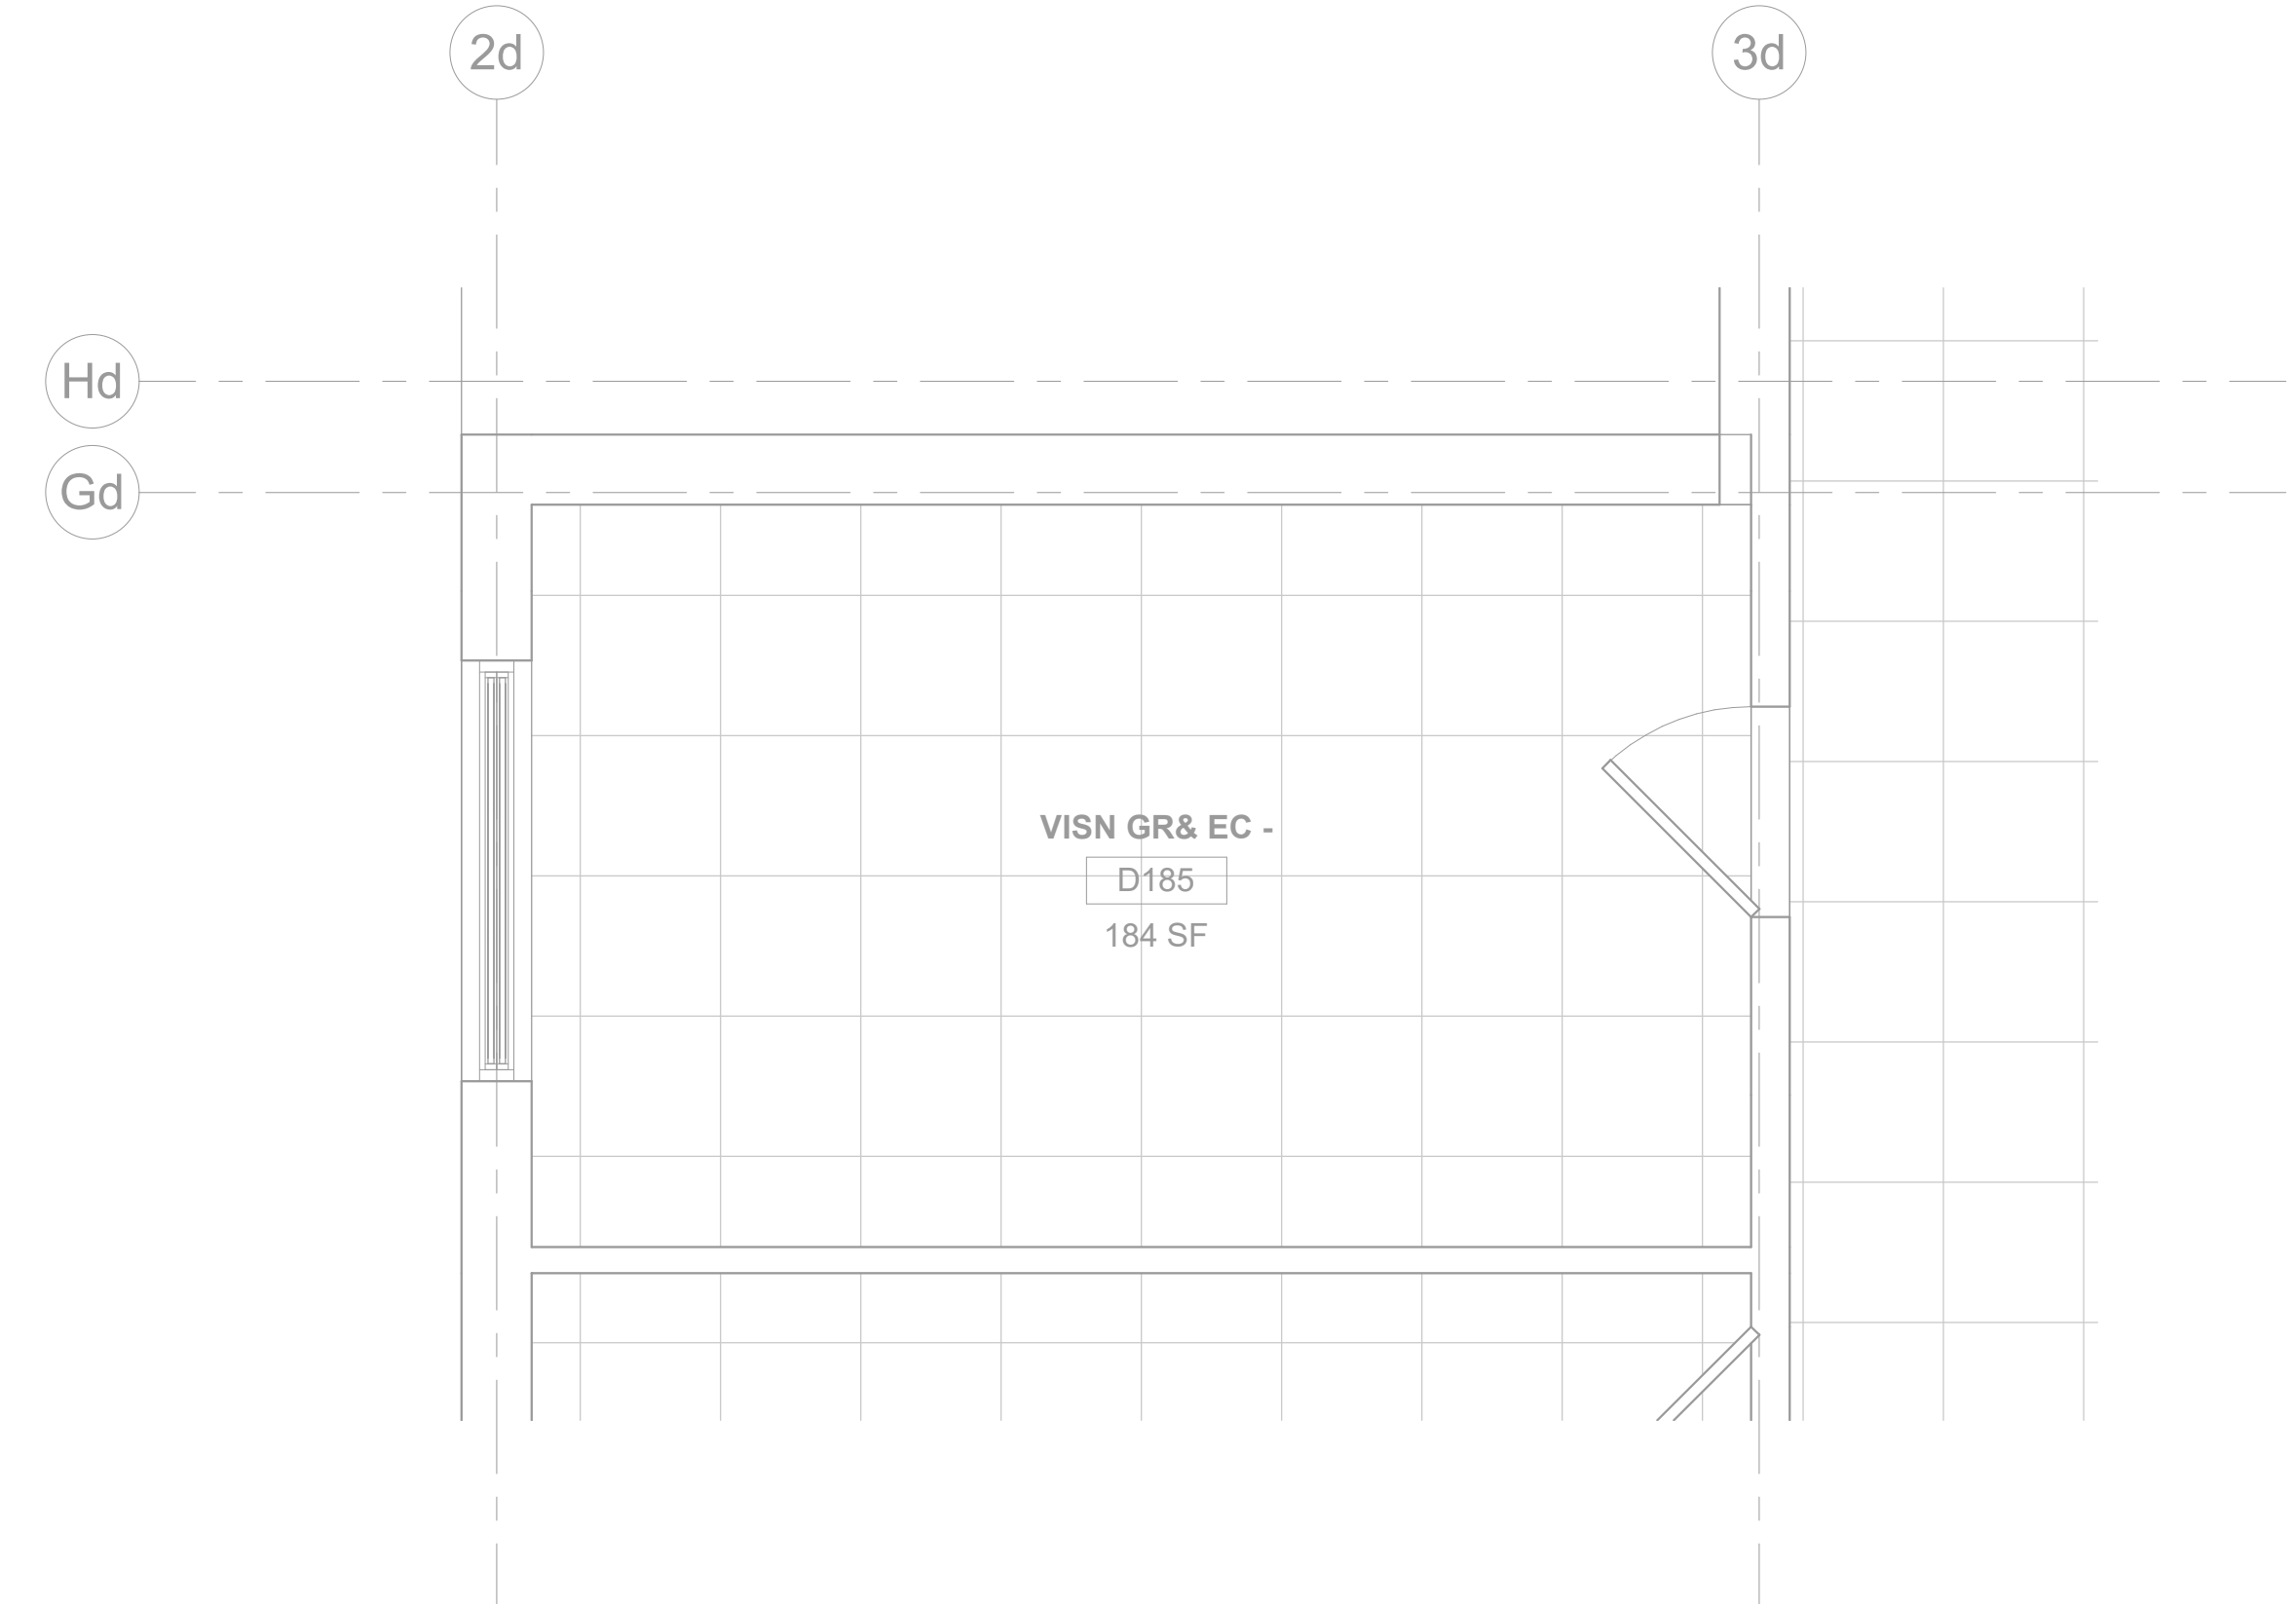


3 RM D185 - DEMOLITION OVERHEAD PLAN

148TN101A 3/8" = 1'-0"

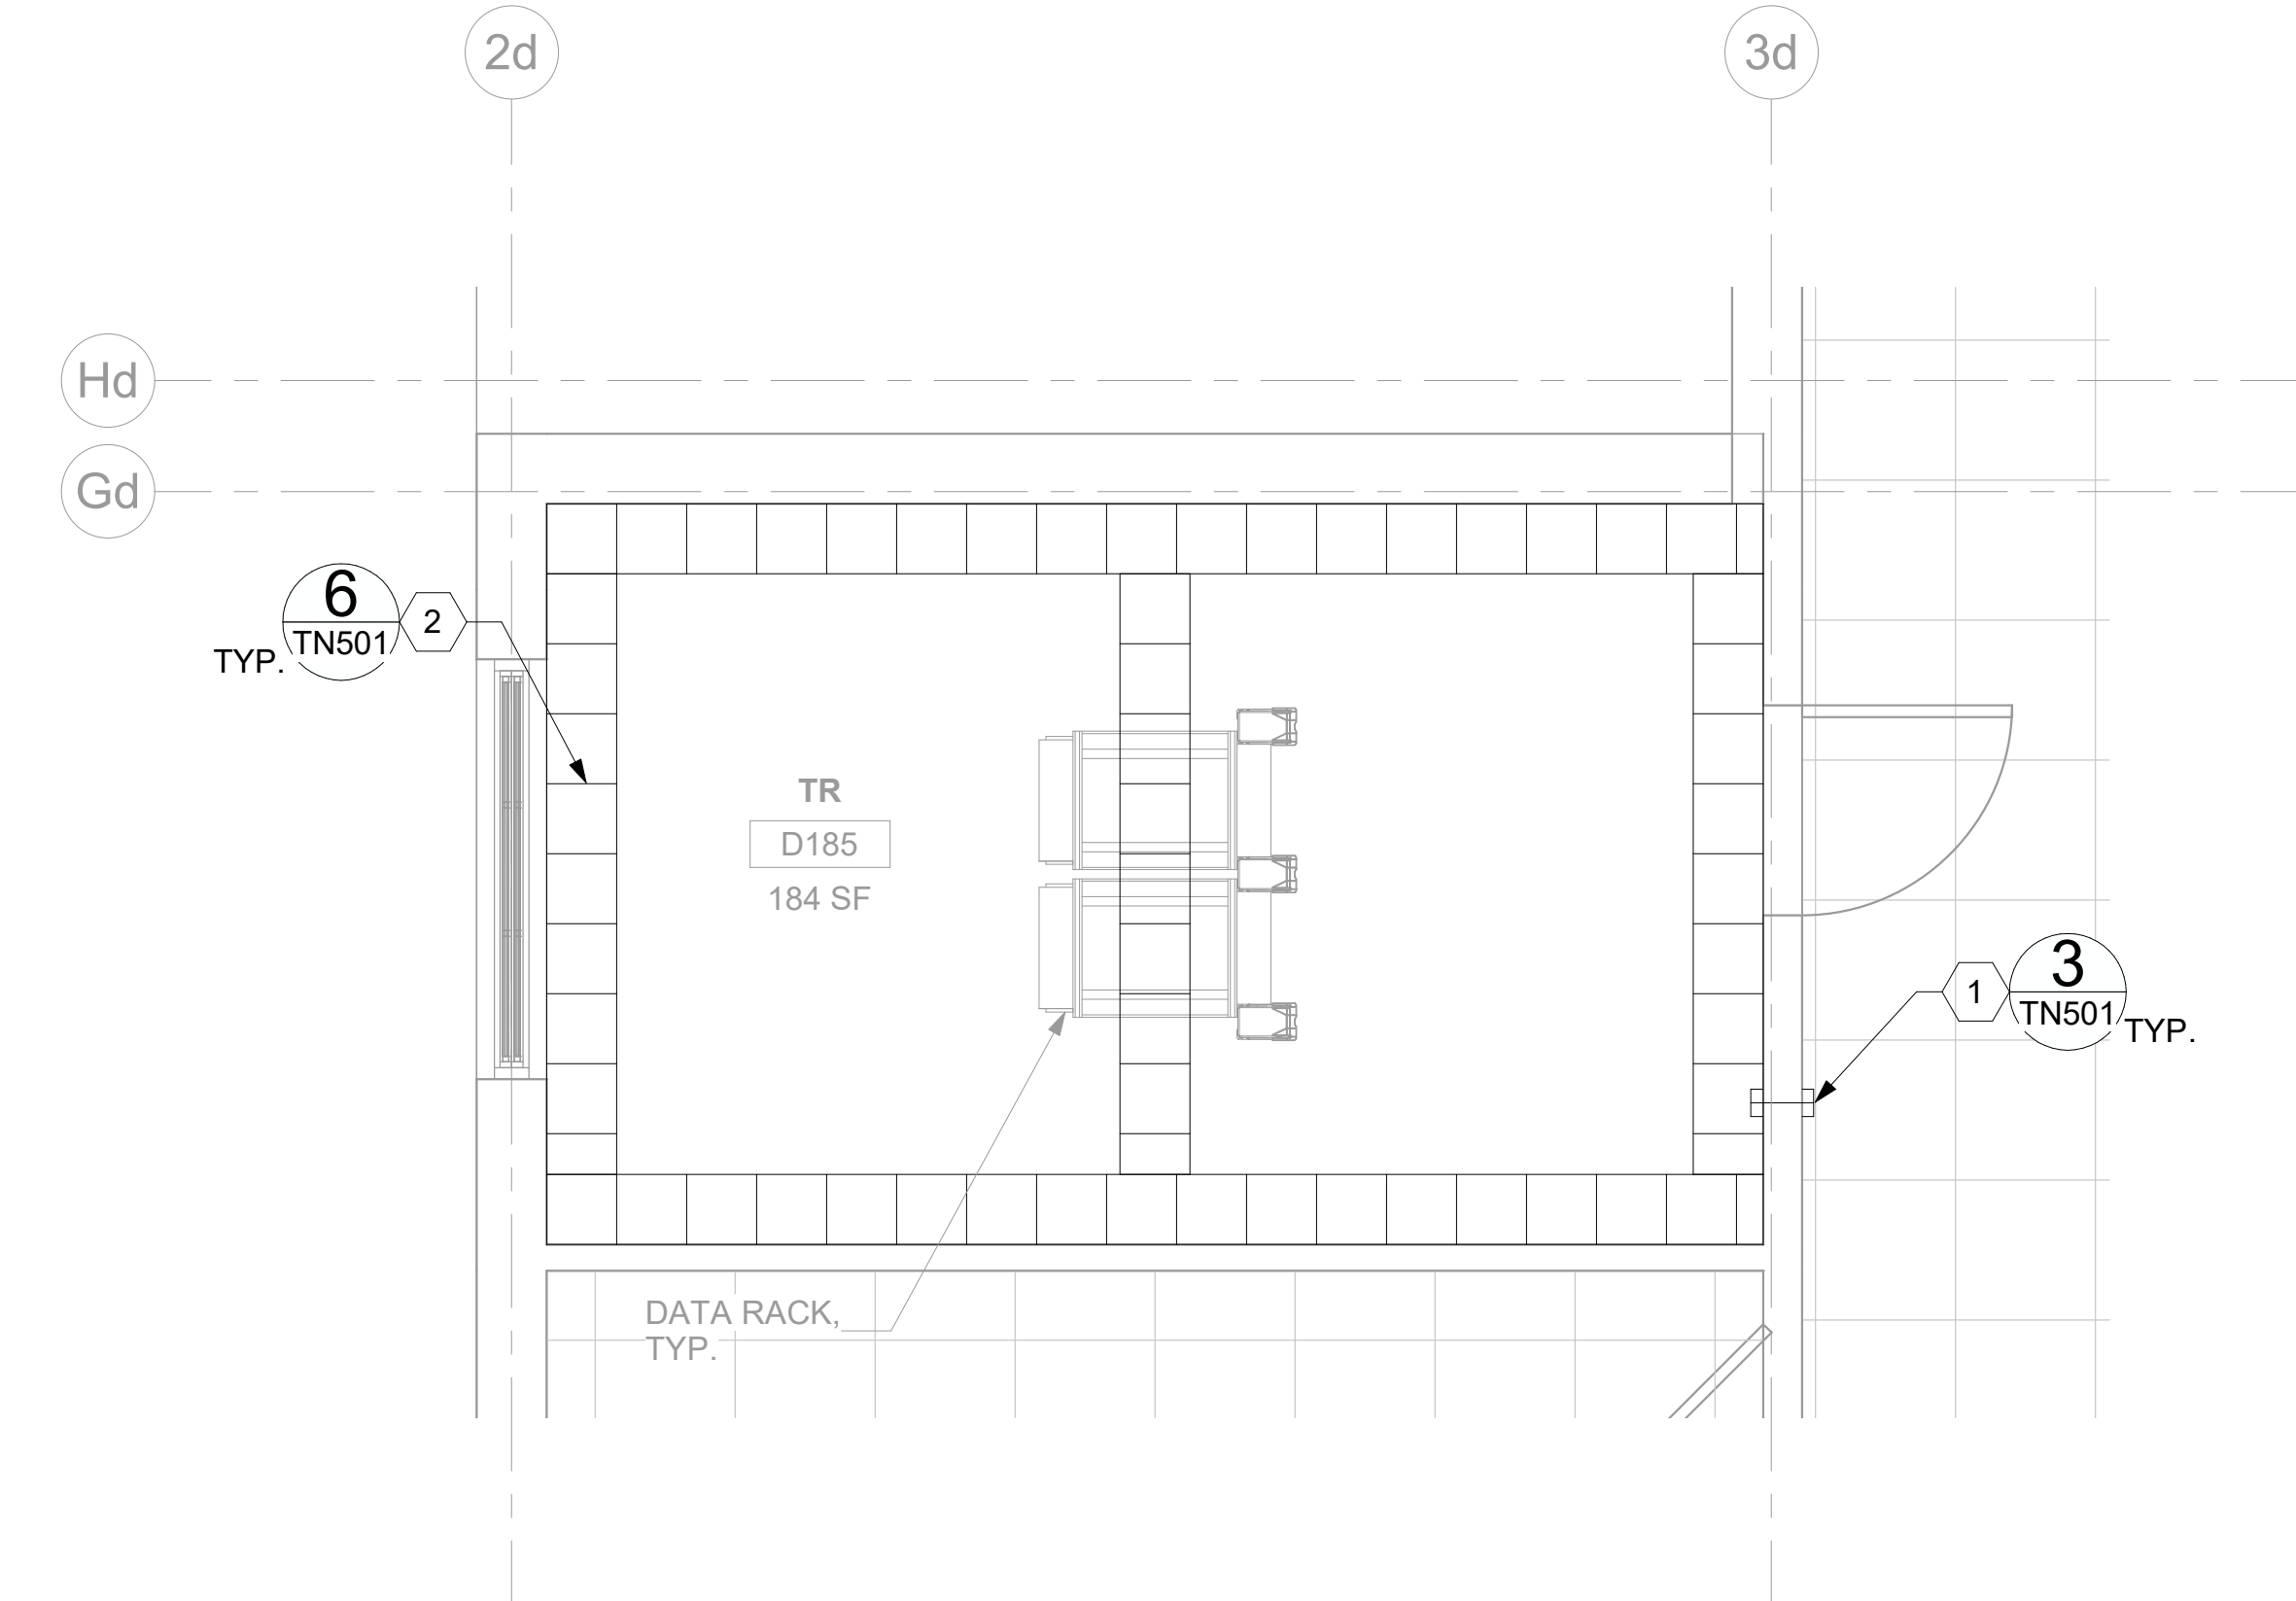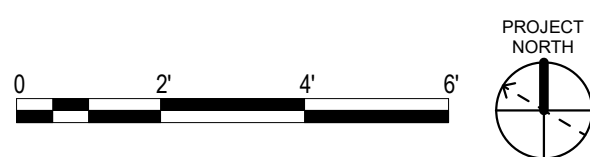

4 RM D185 - OVERHEAD PLAN

148TN101A 3/8" = 1'-0"

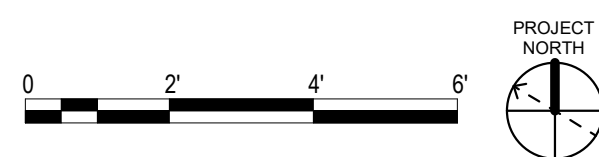

BM 360/599-22-700
Washington EHRMEE - BLDG
148TN

15/07/2025 11:10:53 am

VA FORM 08 - 6231

12345678910

A


B

C



D

E



F

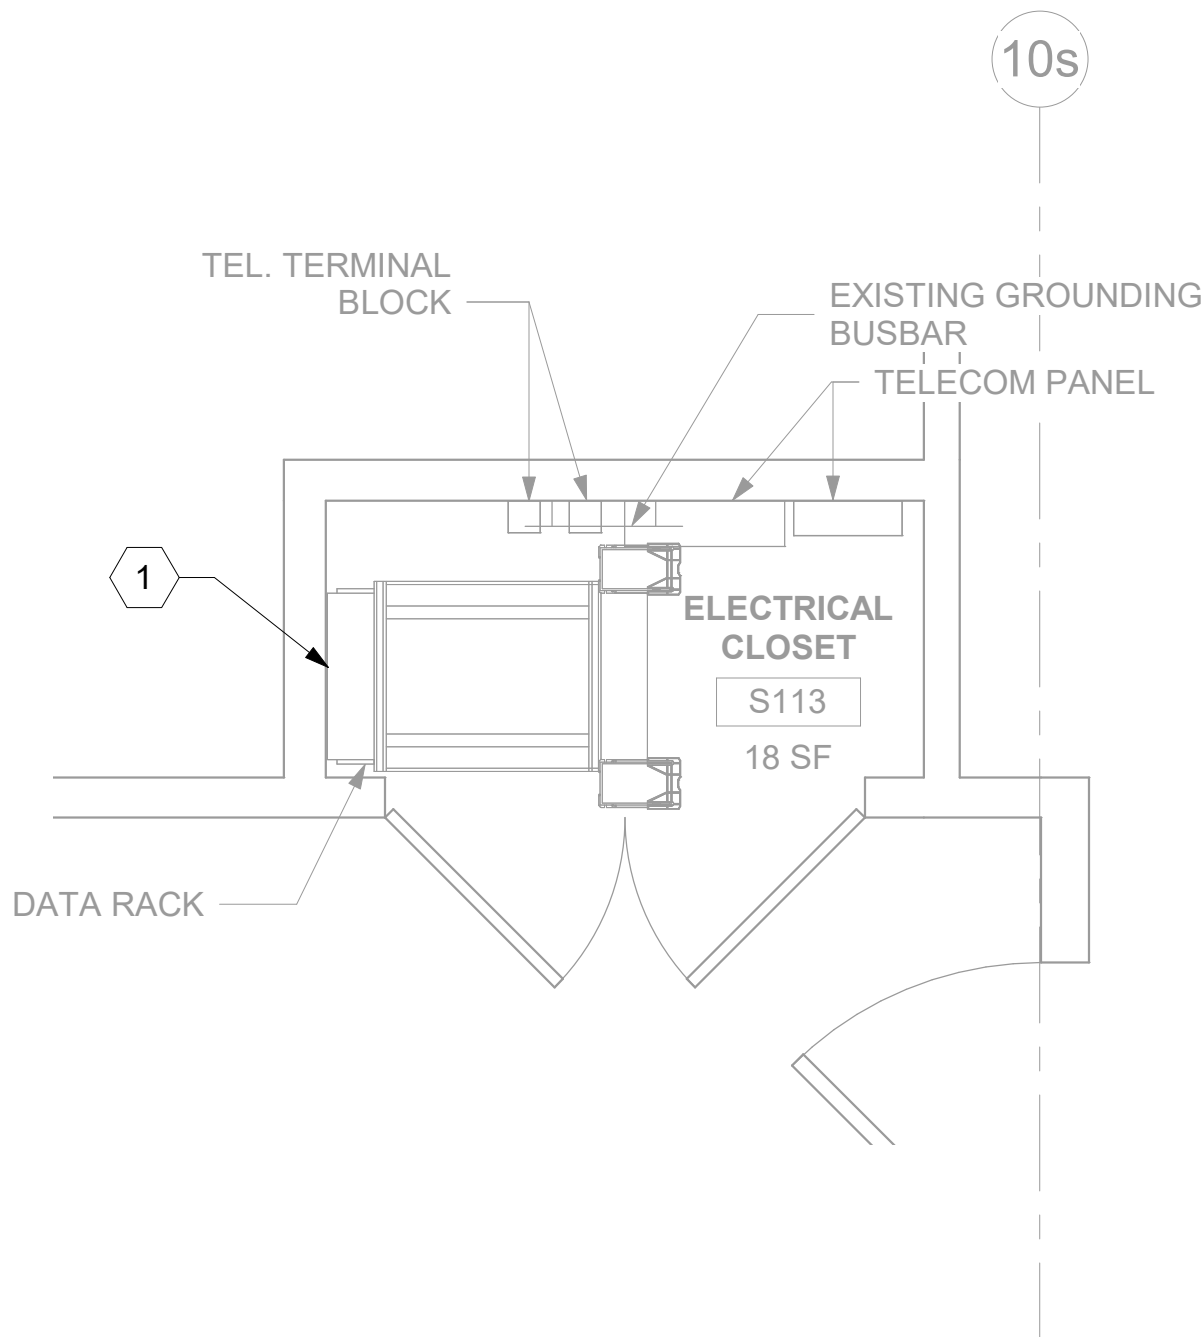



1 RM S113 - DEMOLITION FLOOR PLAN
148TN101A 1/2" = 1'-0"

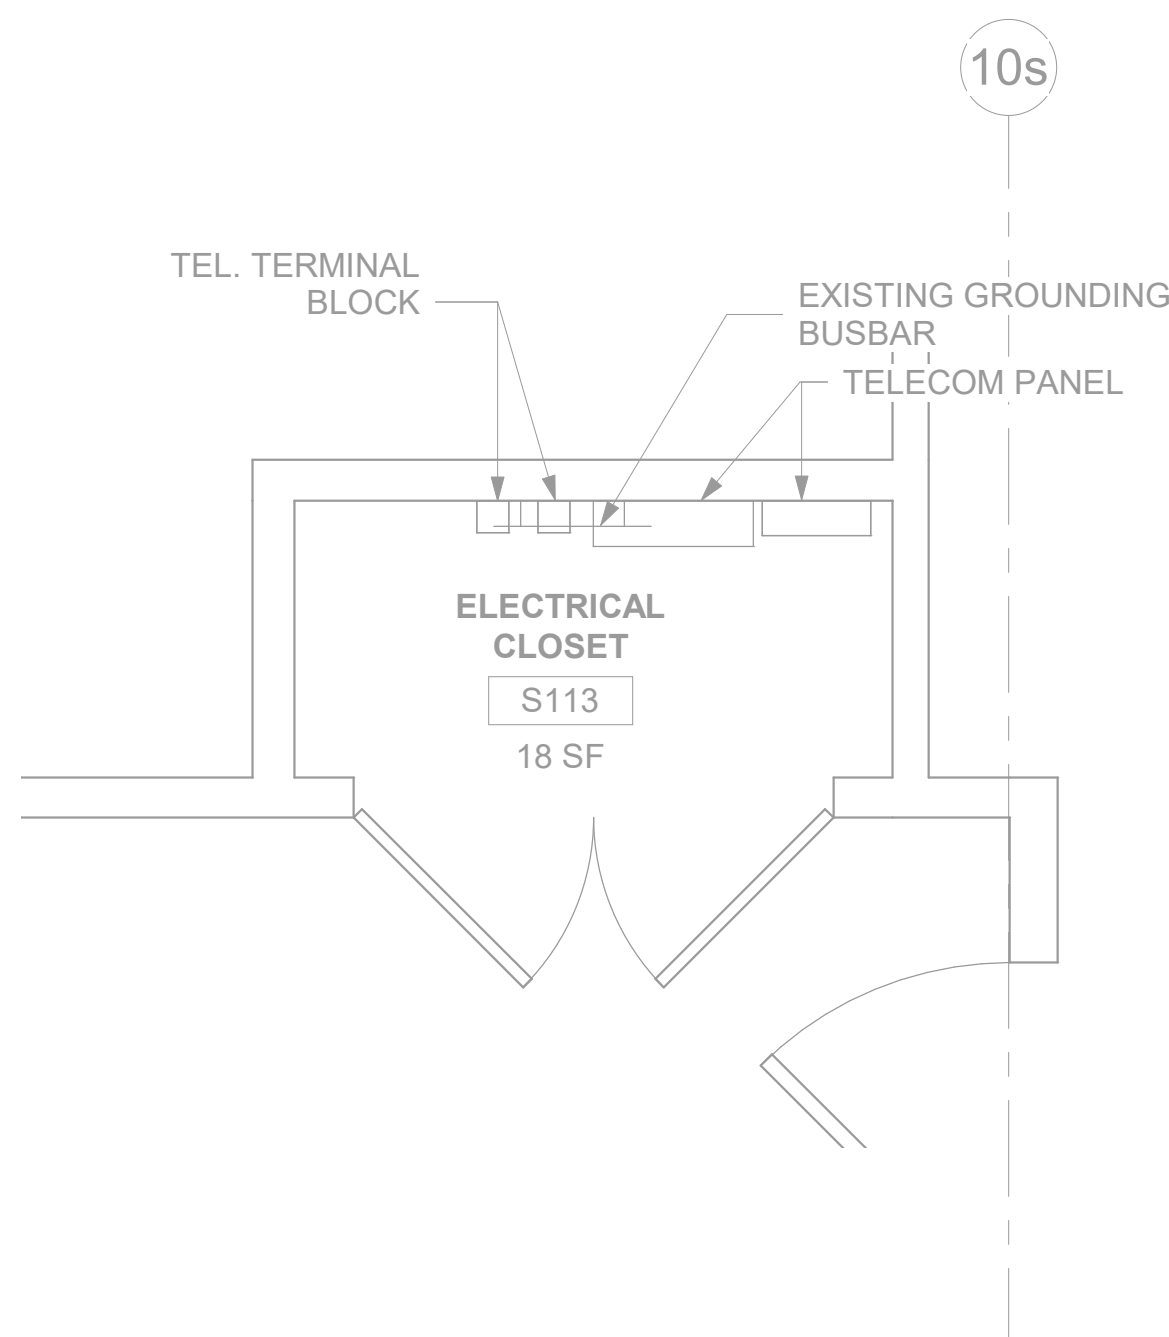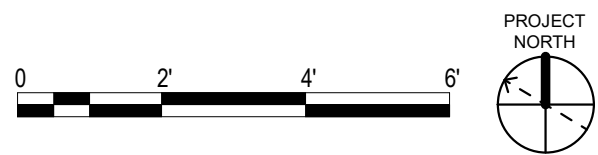


2 RM S113 - TELECOMMUNICATIONS PLAN
148TN101A 1/2" = 1'-0"

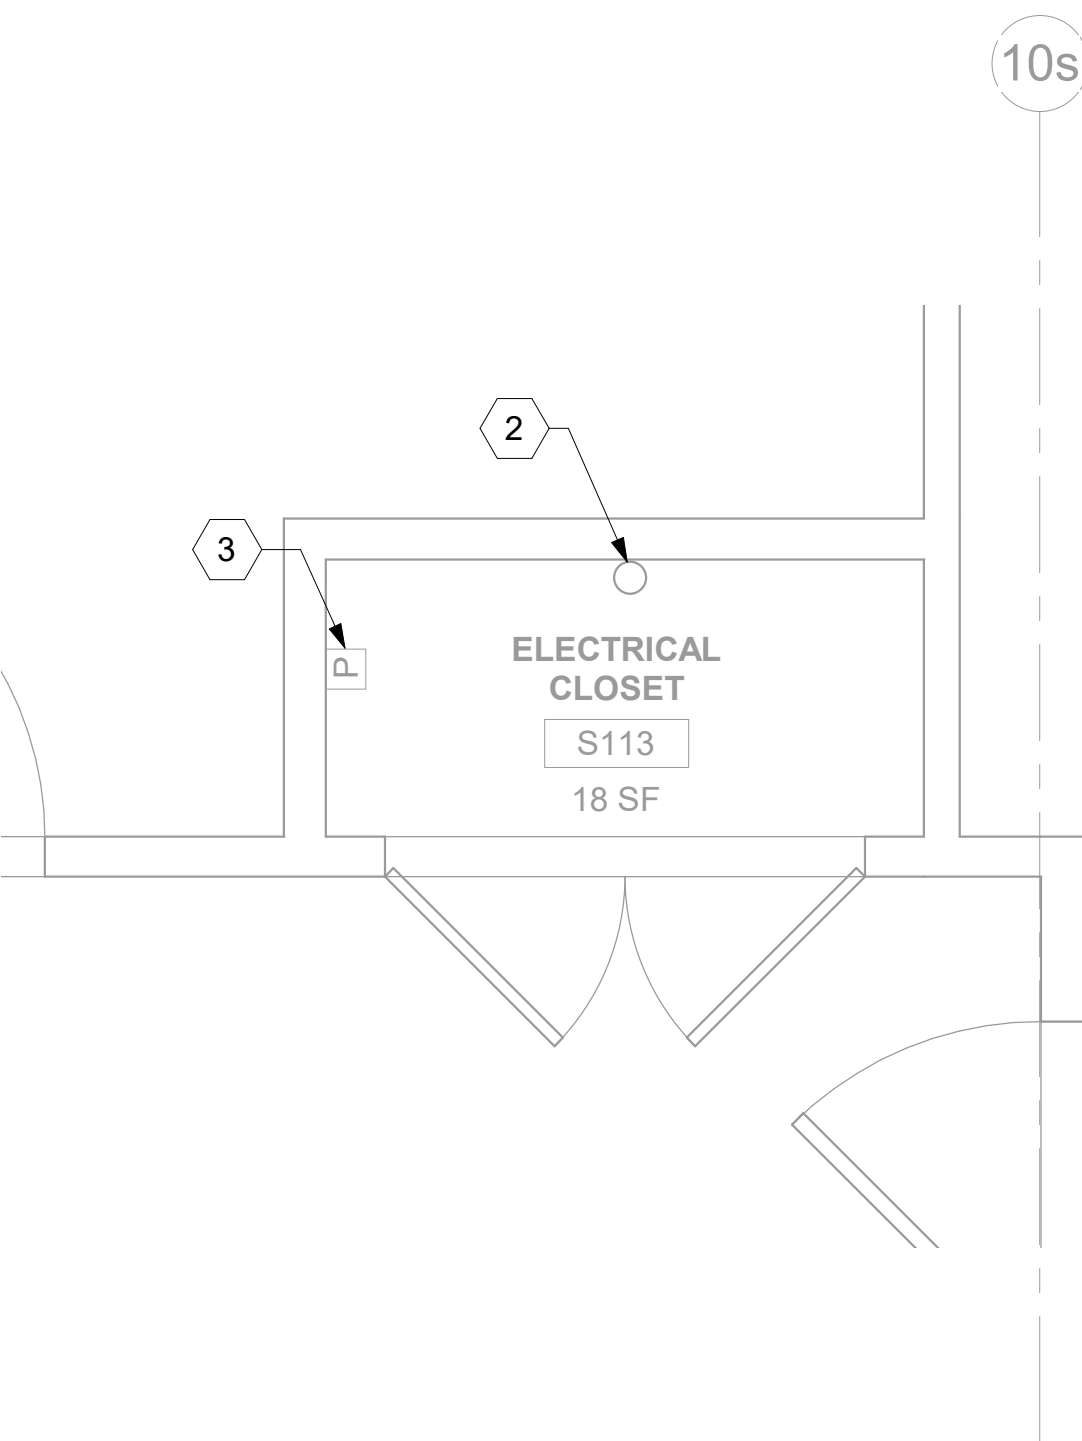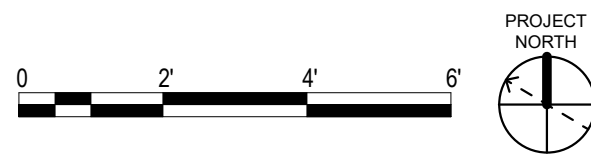

3 RM S113 - DEMOLITION OVERHEAD PLAN
148TN101A 1/2" = 1'-0"

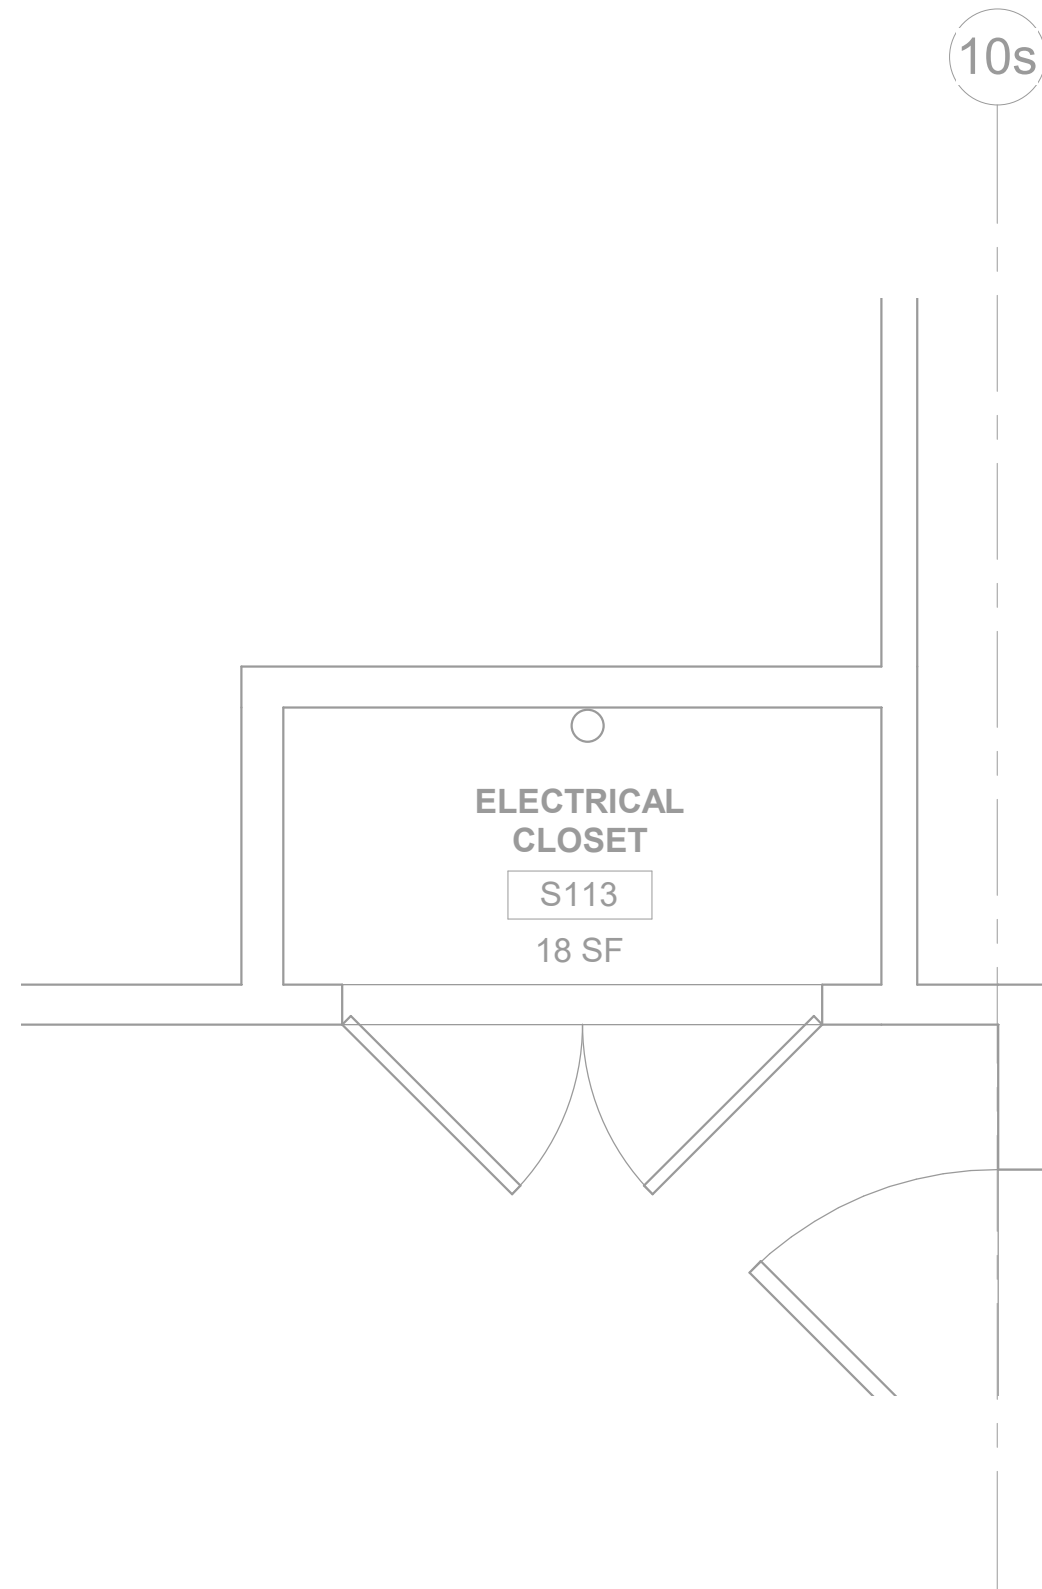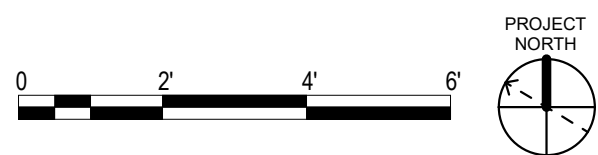

4 RM S113 - OVERHEAD PLAN
148TN101A 1/2" = 1'-0"

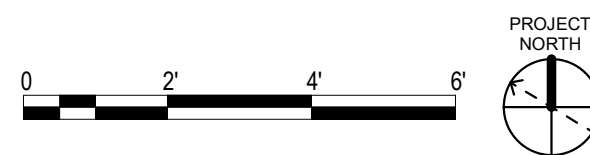


GENERAL NOTES

- PROTECT ALL EXISTING WORK FROM DAMAGE DURING CONSTRUCTION. ANY DAMAGED MATERIALS, SYSTEMS, COMPONENTS, FINISHES AND THE LIKE, SHALL BE REPAIRED OR REPLACED AT THE EXPENSE OF THE CONTRACTOR TO THE ACCEPTANCE OF THE OWNER.
- SEAL ALL INTERIOR WALL AND CEILING PENETRATIONS TO MATCH EXISTING FIRE RATING OR NEW FIRE RATING, IF REQUIRED. COORDINATE WITH ARCHITECTURAL DRAWINGS AS REQUIRED.
- ALL TELECOMMUNICATIONS CABLING CATEGORY 6 AND BELOW SHALL BE REMOVED AND REPLACED WITH CAT6A PORTS AND CABLE QUANTITIES INDICATED, UNLESS NOTED OTHERWISE.
- TELECOMMUNICATIONS CABLES SHALL BE ROUTED IN EXISTING PATHWAY VACATED BY EXISTING CABLING. PROVIDE RACEWAYS TO EXTEND TO ASSOCIATED TR.
- A TELECOMMUNICATIONS OUTLET UPGRADE SHALL INCLUDE, BUT IS NOT LIMITED TO REMOVING AND DISPOSING EXISTING DEVICES AND CABLES; PROVIDING ALL LABOR, MATERIALS, TOOLS, TEST INSTRUMENTS, AND CONSUMABLES REQUIRED FOR THE INSTALLATION, TERMINATION, TESTING, LABELING, AND CERTIFICATION OF A FULLY FUNCTIONAL CATEGORY 6A OUTLET WITH THE PORT QUANTITY INDICATED.
- WHERE NEW DATA OUTLETS ARE BEING PROVIDED AND EXISTING DATA OUTLET CURRENTLY DOES NOT EXIST, PROVIDE (1) 1" CONDUIT FROM NEW BACKBOX TO ACCESSIBLE CEILING SPACE TO SECURELY ROUTE DATA CABLING FROM OUTLET TO TR VIA CABLE TRAY. IF CABLE TRAY IS NON-EXISTENT, EXTEND RACEWAY FROM OUTLET TO TR AS REQUIRED.
- PROVIDE CONDUITS AND SLEEVES AS REQUIRED FOR ROUTING AND INSTALLATION OF HORIZONTAL AND BACKBONE CABLING. PROVIDE FIRE-STOP MATERIALS TO SEAL IN AND AROUND CONDUIT PER CODE. REFER TO ARCHITECTURAL DRAWINGS FOR PARTITION TYPES AND WALL HEIGHTS.
- ALL TELECOMMUNICATION ROOMS SHALL BE PROVIDED WITH FIRE-RATED PLYWOOD BACKBOARDS. REFERENCE EXACT PLACEMENTS WITH ARCHITECTURE DRAWINGS AS REQUIRED.
- ANY LIVE SYSTEMS IN DEMO'D TR'S MUST REMAIN LIVE. CONTRACTOR TO COORDINATE WITH THE STATION TO IDENTIFY SYSTEMS THAT ARE LIVE. IF SYSTEMS ARE LIVE; INSTALL NEW CABLE FROM DEMO'D TR TO NEW TR. REFER TO DETAIL '3' ON TN506.

KEY NOTES

- EXISTING DATA RACK TO BE DECOMMISSIONED BY VA. CONTRACTOR SHALL COORDINATE WITH VA AS REQUIRED.
- EXISTING VERTICAL CABLING SLEEVES (QTY = 18) TO BE PRESERVED. EXISTING FIBER OPTIC AND/OR EXISTING VERTICAL CABLING RELATED TO EXISTING TR RACKS TO BE DEMOLISHED.
- EXISTING PENETRATIONS WITH CABLING TO BE REMOVED. CONTRACTOR SHALL PATCH AND FIREPROOF OPENINGS. COORDINATE WITH ARCHITECTURAL DRAWINGS AND SPECIFICATIONS.

KEY PLAN

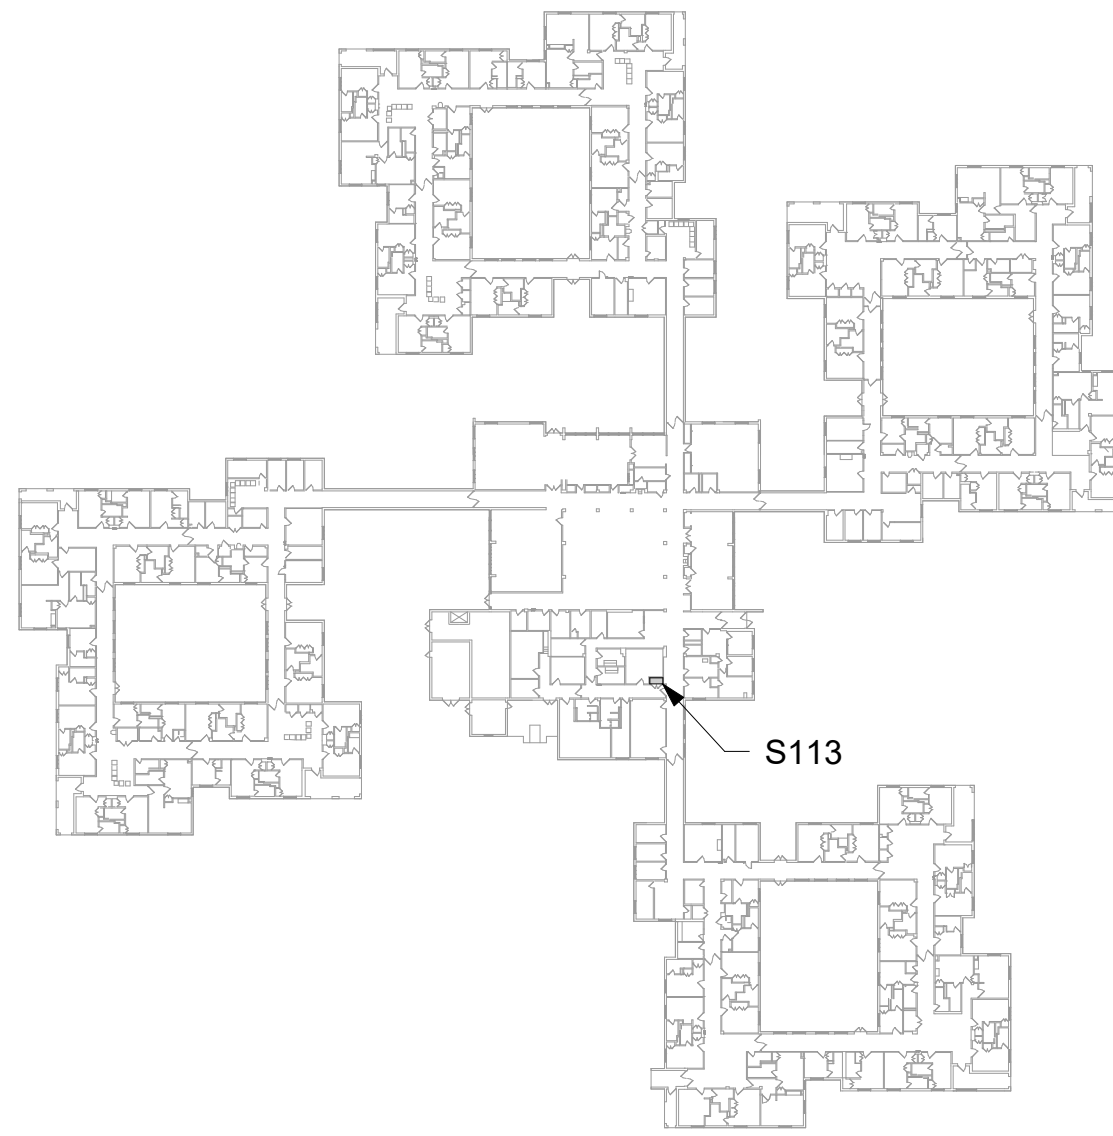

AREA SHOWN



Revisions:	Date:

CONSULTANT
ENGINEERING DISCIPLINE:

ARCHITECT/ENGINEER OF RECORD

A/E:
SPEES DESIGN BUILD
23830 PACIFIC HIGHWAY S. SUITE 203
KENT, WA 98032



STAMP



Office of
Construction
and Facilities
Management



U.S. Department
of Veterans Affairs

Drawing Title
BLDG 148 - LEVEL 01 - ENLARGED
TELECOMMUNICATIONS PLANS

Approved:

Phase
100% CONSTRUCTION
DOCUMENTS

FULLY SPRINKLERED

Project Title
EHRM INFRASTRUCTURE
UPGRADES - HAMPTON

Location
HAMPTON VA MEDICAL CENTER, HAMPTON, VIRGINIA

Issue Date
07/18/2025

Checked
KG


Drawn
BCL/GPB

Project Number
590-22-700
Building Number
148



Drawing Number
148TN401e

609 of 713



12345678910

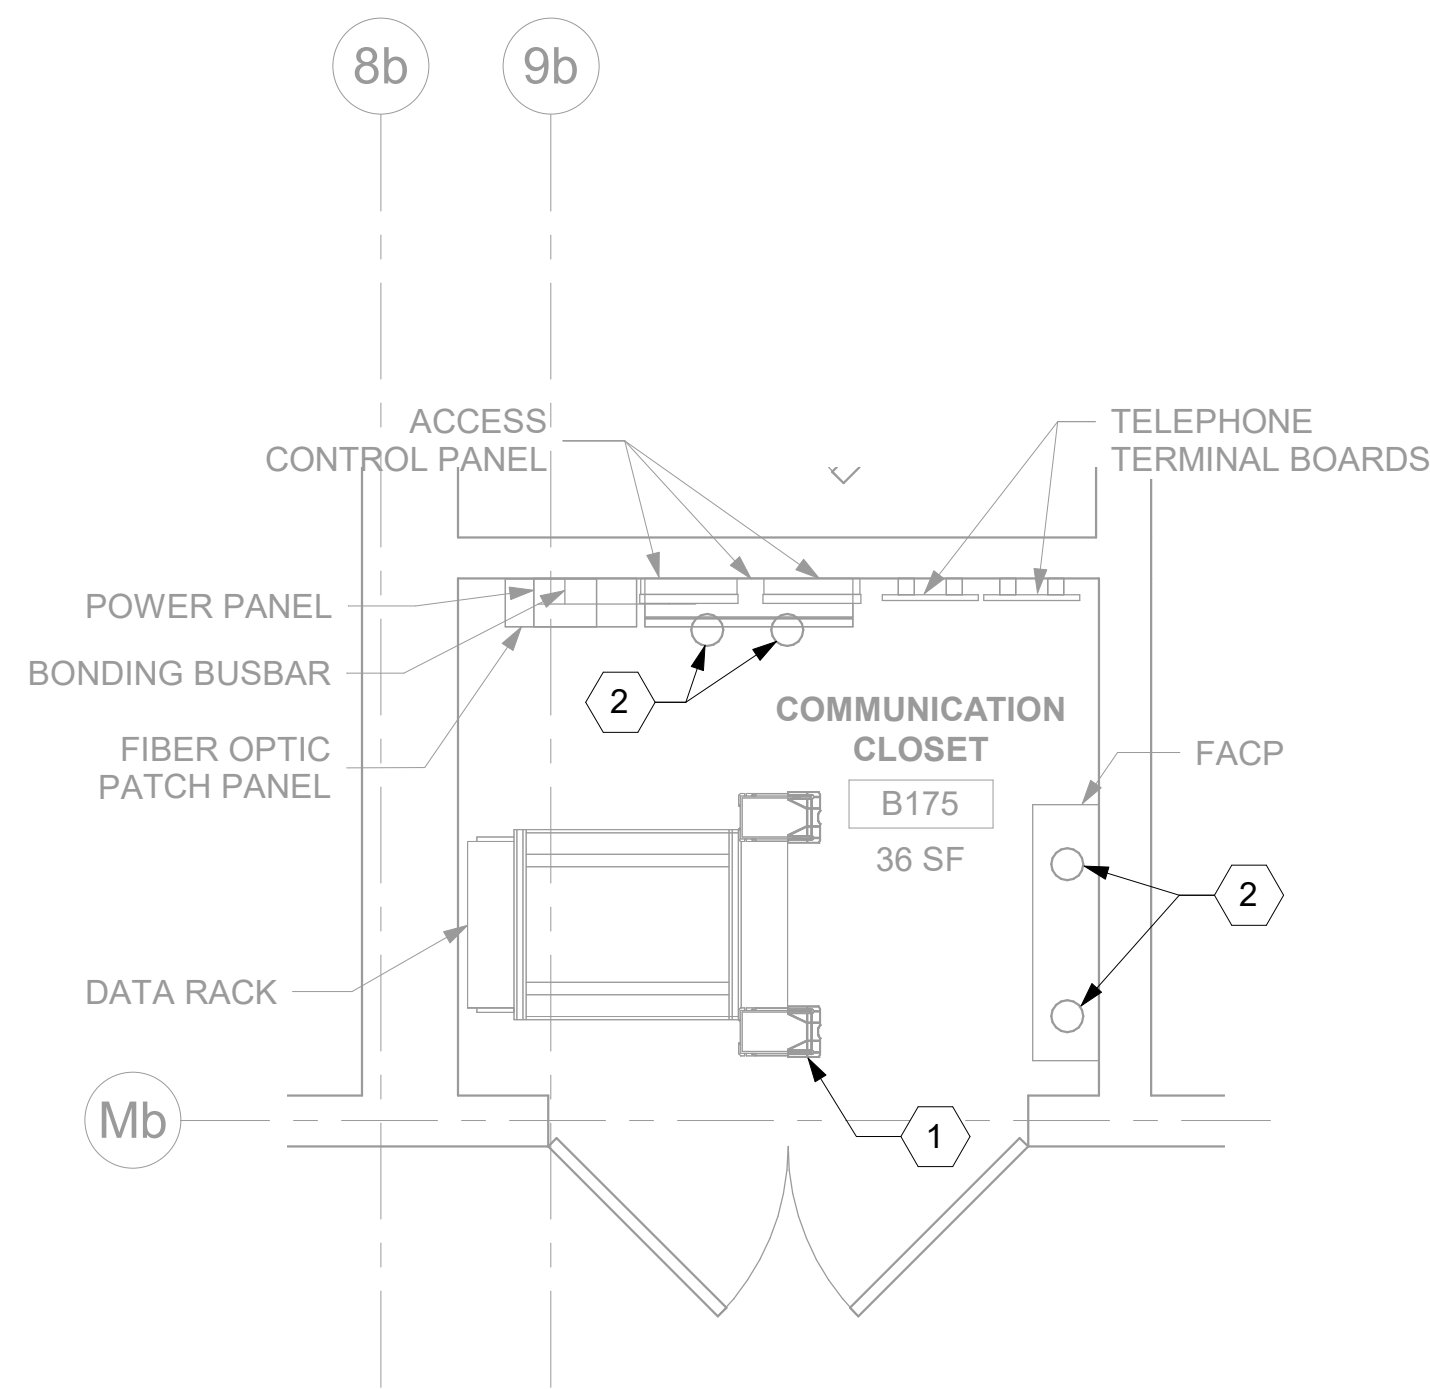



1 RM B175 - DEMOLITION FLOOR PLAN
148TN101B 1/2" = 1'-0"

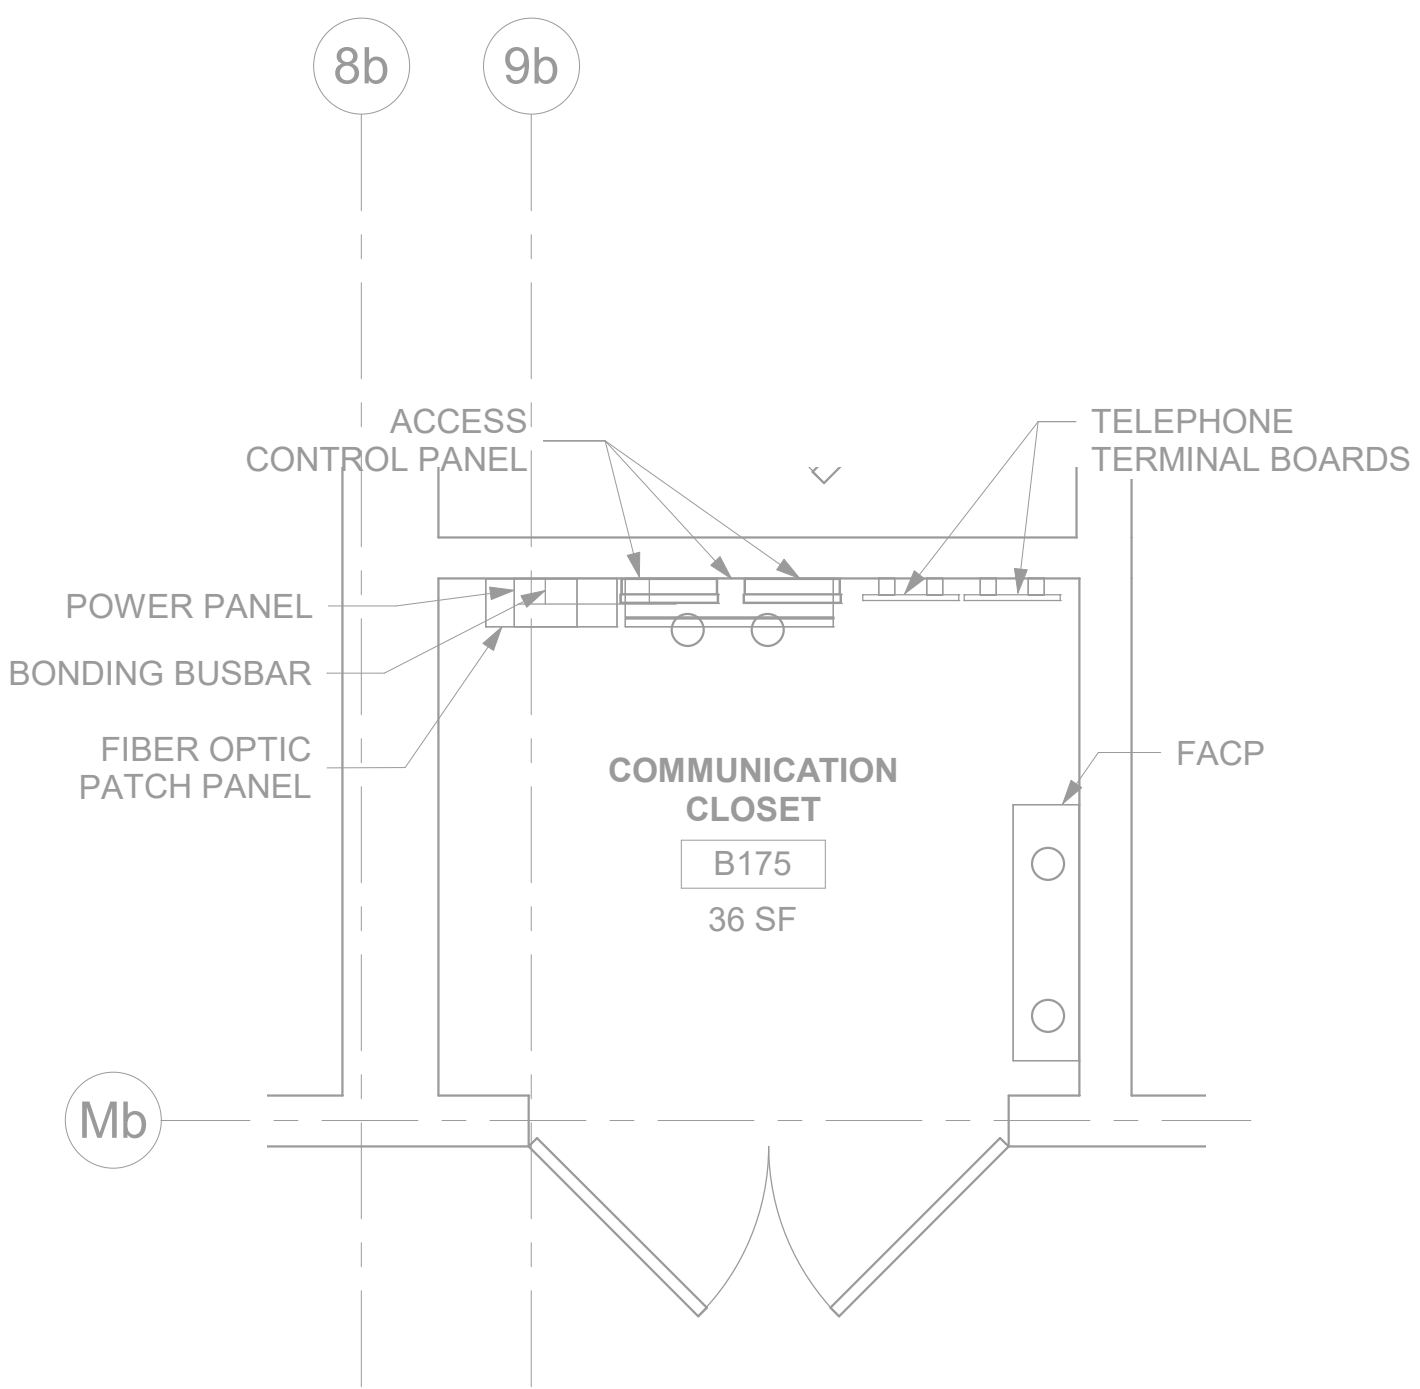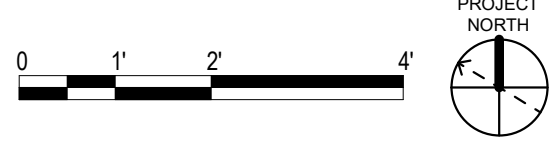


2 RM B175 - TELECOMMUNICATIONS PLAN
148TN101B 1/2" = 1'-0"

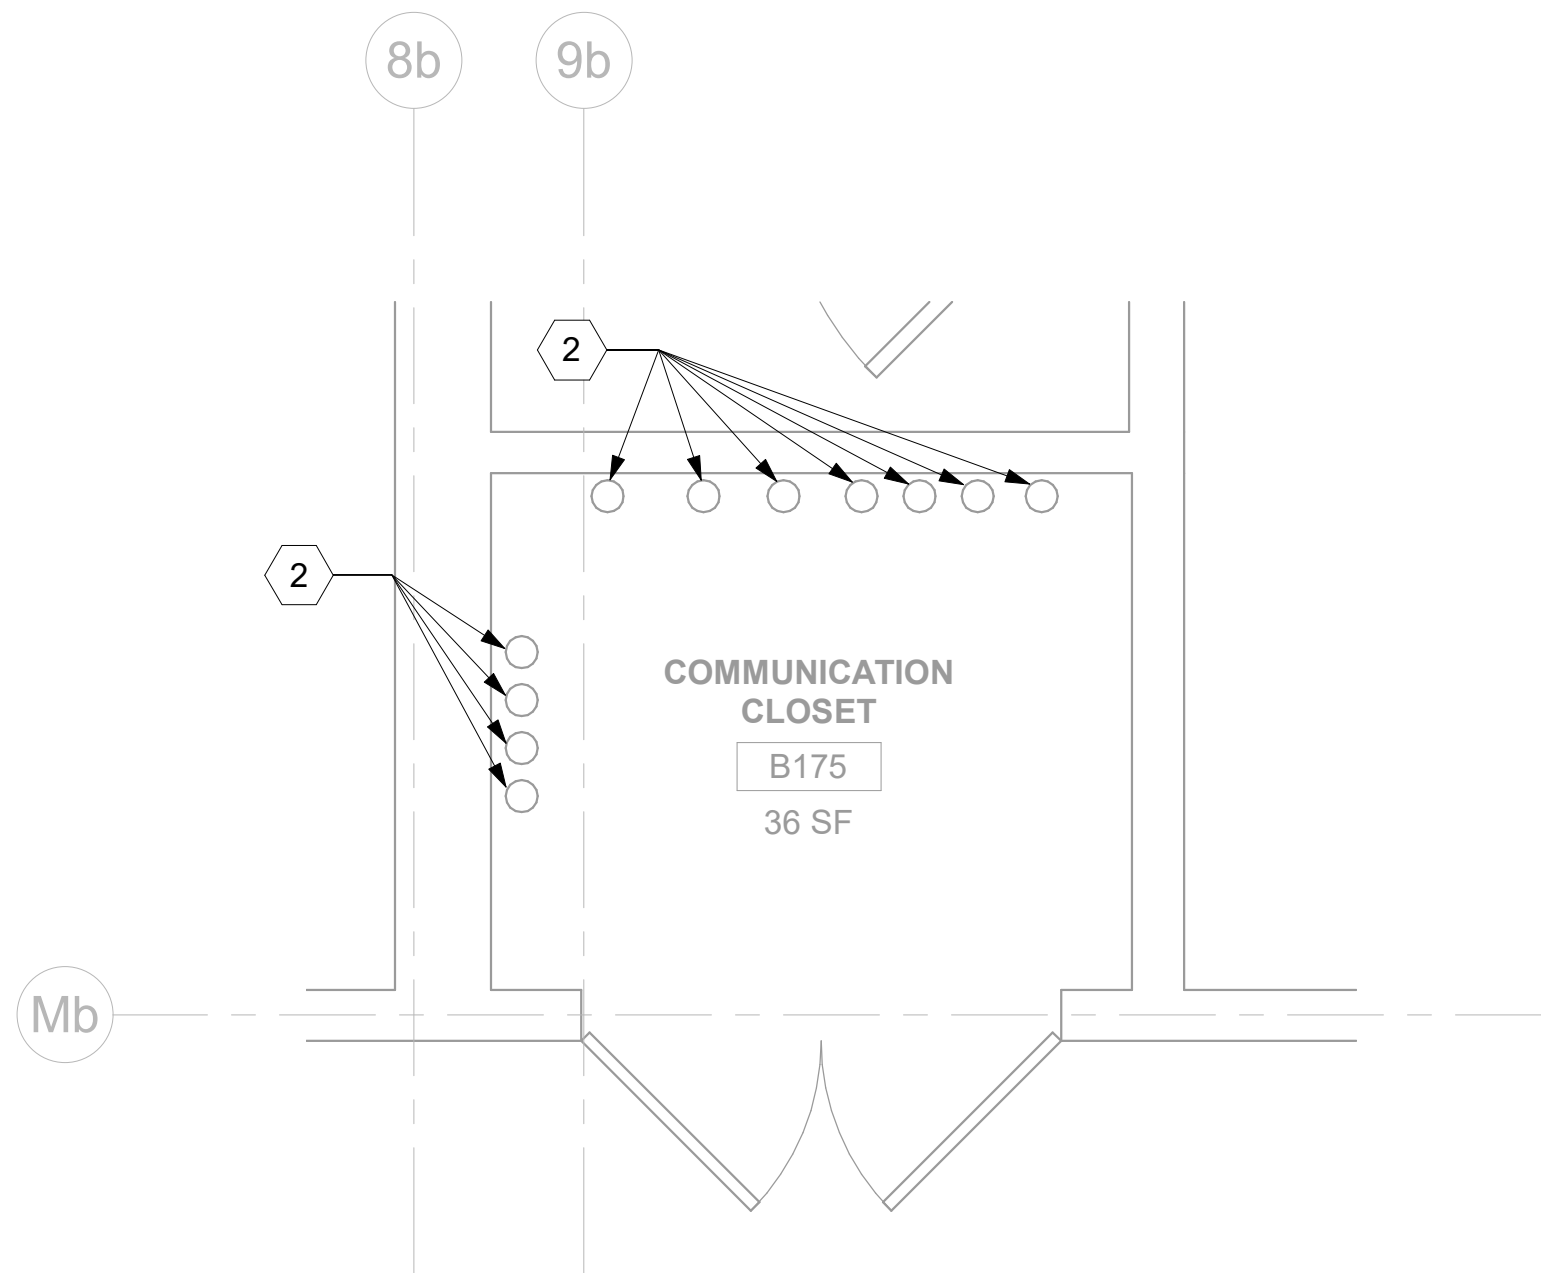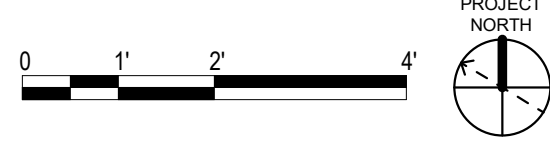

3 RM B175 - DEMOLITION OVERHEAD PLAN
148TN101A 1/2" = 1'-0"

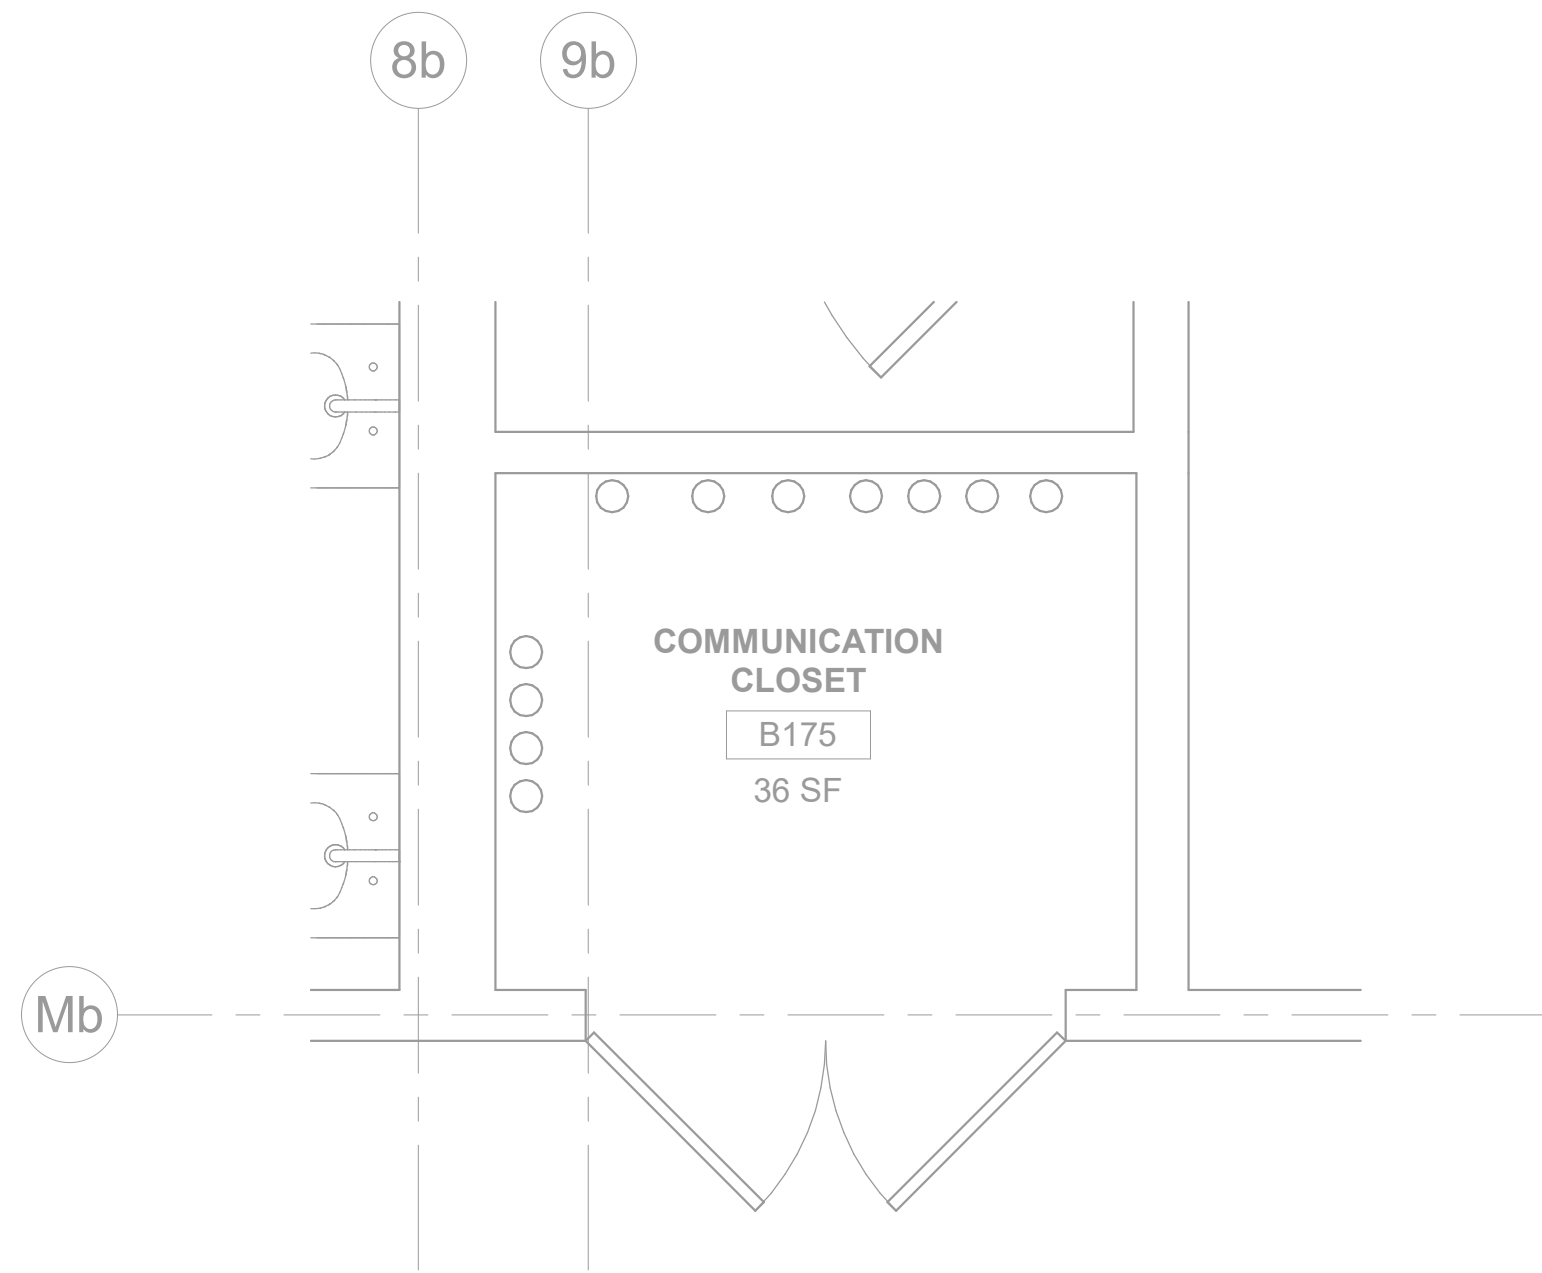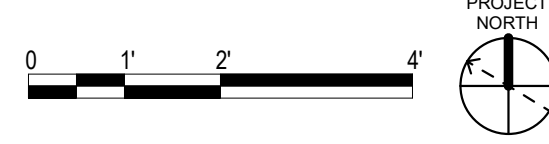

4 RM B175 - OVERHEAD PLAN
148TN101A 1/2" = 1'-0"

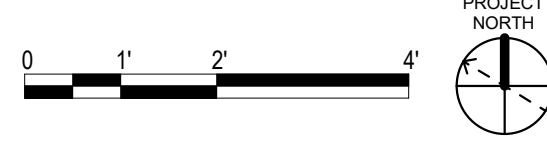


GENERAL NOTES

- PROTECT ALL EXISTING WORK FROM DAMAGE DURING CONSTRUCTION. ANY DAMAGED MATERIALS, SYSTEMS, COMPONENTS, FINISHES AND THE LIKE, SHALL BE REPAIRED OR REPLACED AT THE EXPENSE OF THE CONTRACTOR TO THE ACCEPTANCE OF THE OWNER.
- SEAL ALL INTERIOR WALL AND CEILING PENETRATIONS TO MATCH EXISTING FIRE RATING OR NEW FIRE RATING, IF REQUIRED. COORDINATE WITH ARCHITECTURAL DRAWINGS AS REQUIRED.
- ALL TELECOMMUNICATIONS CABLING CATEGORY 6 AND BELOW SHALL BE REMOVED AND REPLACED WITH CAT6A PORTS AND CABLE QUANTITIES INDICATED, UNLESS NOTED OTHERWISE.
- TELECOMMUNICATIONS CABLES SHALL BE ROUTED IN EXISTING PATHWAY VACATED BY EXISTING CABLING. PROVIDE RACEWAYS TO EXTEND TO ASSOCIATED TR.
- A TELECOMMUNICATIONS OUTLET UPGRADE SHALL INCLUDE, BUT IS NOT LIMITED TO REMOVING AND DISPOSING EXISTING DEVICES AND CABLES; PROVIDING ALL LABOR, MATERIALS, TOOLS, TEST INSTRUMENTS, AND CONSUMABLES REQUIRED FOR THE INSTALLATION, TERMINATION, TESTING, LABELING, AND CERTIFICATION OF A FULLY FUNCTIONAL CATEGORY 6A OUTLET WITH THE PORT QUANTITY INDICATED.
- WHERE NEW DATA OUTLETS ARE BEING PROVIDED AND EXISTING DATA OUTLET CURRENTLY DOES NOT EXIST, PROVIDE (1) 1" CONDUIT FROM NEW BACKBOX TO ACCESSIBLE CEILING SPACE TO SECURELY ROUTE DATA CABLING FROM OUTLET TO TR VIA CABLE TRAY. IF CABLE TRAY IS NON-EXISTENT, EXTEND RACEWAY FROM OUTLET TO TR AS REQUIRED.
- PROVIDE CONDUITS AND SLEEVES AS REQUIRED FOR ROUTING AND INSTALLATION OF HORIZONTAL AND BACKBONE CABLING. PROVIDE FIRE-STOP MATERIALS TO SEAL IN AND AROUND CONDUIT PER CODE. REFER TO ARCHITECTURAL DRAWINGS FOR PARTITION TYPES AND WALL HEIGHTS.
- ALL TELECOMMUNICATION ROOMS SHALL BE PROVIDED WITH FIRE-RATED PLYWOOD BACKBOARDS. REFERENCE EXACT PLACEMENTS WITH ARCHITECTURE DRAWINGS AS REQUIRED.
- ANY LIVE SYSTEMS IN DEMO'D TR'S MUST REMAIN LIVE. CONTRACTOR TO COORDINATE WITH THE STATION TO IDENTIFY SYSTEMS THAT ARE LIVE. IF SYSTEMS ARE LIVE; INSTALL NEW CABLE FROM DEMO'D TR TO NEW TR. REFER TO DETAIL '3' ON TN506.

KEY NOTES

- EXISTING DATA RACK TO BE DECOMMISSIONED BY VA. CONTRACTOR SHALL COORDINATE WITH VA AS REQUIRED.
- EXISTING VERTICAL CABLING SLEEVE TO BE PRESERVED. EXISTING FIBER OPTIC AND/OR EXISTING VERTICAL CABLING RELATED TO EXISTING TR RACKS TO BE DEMOLISHED.

KEY PLAN

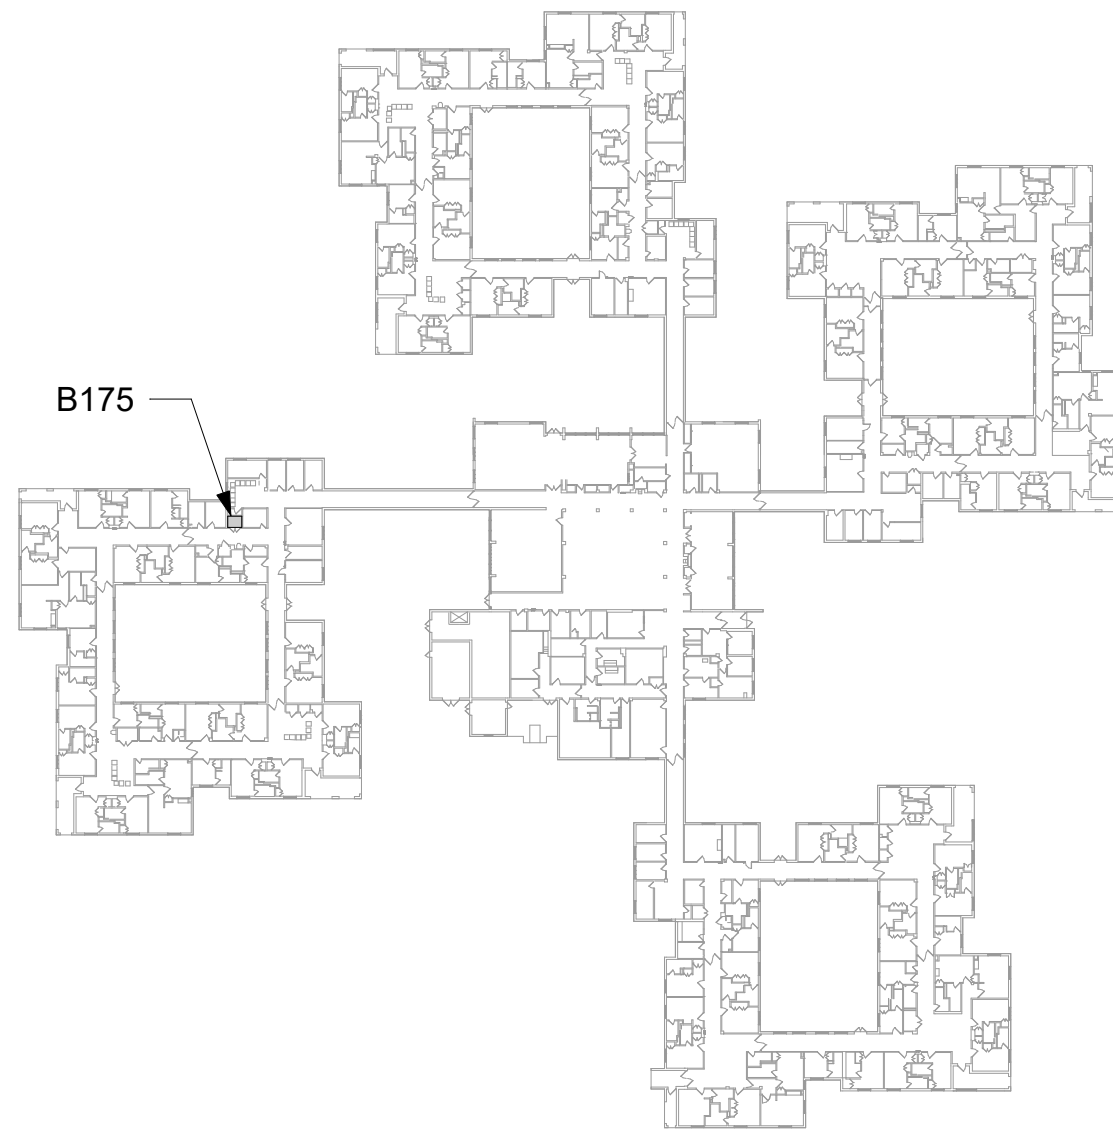

AREA SHOWN



		CONSULTANT	ARCHITECT/ENGINEER OF RECORD	STAMP	Office of Construction and Facilities Management VA U.S. Department of Veterans Affairs	Drawing Title	Phase	Project Title	Project Number		
		ENGINEERING DISCIPLINE:	A/E: SPEES DESIGN BUILD 23830 PACIFIC HIGHWAY S. SUITE 203 KENT, WA 98032			BLDG 148 - LEVEL 01 - ENLARGED TELECOMMUNICATIONS PLANS	100% CONSTRUCTION DOCUMENTS	EHRM INFRASTRUCTURE UPGRADES - HAMPTON	590-22-700		
									Building Number		
									148		
									Drawing Number		
						Approved:	FULLY SPRINKLERED	Location HAMPTON VA MEDICAL CENTER, HAMPTON, VIRGINIA	148TN401f		
Revisions:	Date:							Issue Date 07/18/2025	Checked KG	Drawn BCL/GPB	610 of 713

A

B

C

D

E

F

A

B

C

D

E

F


GENERAL NOTES

- PROTECT ALL EXISTING WORK FROM DAMAGE DURING CONSTRUCTION. ANY DAMAGED MATERIALS, SYSTEMS, COMPONENTS, FINISHES AND THE LIKE, SHALL BE REPAIRED OR REPLACED AT THE EXPENSE OF THE CONTRACTOR TO THE ACCEPTANCE OF THE OWNER.
- SEAL ALL INTERIOR WALL AND CEILING PENETRATIONS TO MATCH EXISTING FIRE RATING OR NEW FIRE RATING, IF REQUIRED. COORDINATE WITH ARCHITECTURAL DRAWINGS AS REQUIRED.
- ALL TELECOMMUNICATIONS CABLING CATEGORY 6 AND BELOW SHALL BE REMOVED AND REPLACED WITH CAT6A PORTS AND CABLE QUANTITIES INDICATED, UNLESS NOTED OTHERWISE.
- TELECOMMUNICATIONS CABLES SHALL BE ROUTED IN EXISTING PATHWAY VACATED BY EXISTING CABLING. PROVIDE RACEWAYS TO EXTEND TO ASSOCIATED TR.
- A TELECOMMUNICATIONS OUTLET UPGRADE SHALL INCLUDE, BUT IS NOT LIMITED TO REMOVING AND DISPOSING EXISTING DEVICES AND CABLES; PROVIDING ALL LABOR, MATERIALS, TOOLS, TEST INSTRUMENTS, AND CONSUMABLES REQUIRED FOR THE INSTALLATION, TERMINATION, TESTING, LABELING, AND CERTIFICATION OF A FULLY FUNCTIONAL CATEGORY 6A OUTLET WITH THE PORT QUANTITY INDICATED.
- WHERE NEW DATA OUTLETS ARE BEING PROVIDED AND EXISTING DATA OUTLET CURRENTLY DOES NOT EXIST, PROVIDE (1) 1" CONDUIT FROM NEW BACKBOX TO ACCESSIBLE CEILING SPACE TO SECURELY ROUTE DATA CABLING FROM OUTLET TO TR VIA CABLE TRAY. IF CABLE TRAY IS NON-EXISTENT, EXTEND RACEWAY FROM OUTLET TO TR AS REQUIRED.
- PROVIDE CONDUITS AND SLEEVES AS REQUIRED FOR ROUTING AND INSTALLATION OF HORIZONTAL AND BACKBONE CABLING. PROVIDE FIRE-STOP MATERIALS TO SEAL IN AND AROUND CONDUIT PER CODE. REFER TO ARCHITECTURAL DRAWINGS FOR PARTITION TYPES AND WALL HEIGHTS.
- ALL TELECOMMUNICATION ROOMS SHALL BE PROVIDED WITH FIRE-RATED PLYWOOD BACKBOARDS. REFERENCE EXACT PLACEMENTS WITH ARCHITECTURE DRAWINGS AS REQUIRED.
- ANY LIVE SYSTEMS IN DEMO'D TR'S MUST REMAIN LIVE. CONTRACTOR TO COORDINATE WITH THE STATION TO IDENTIFY SYSTEMS THAT ARE LIVE. IF SYSTEMS ARE LIVE; INSTALL NEW CABLE FROM DEMO'D TR TO NEW TR. REFER TO DETAIL '3' ON TN506.


KEY NOTES

- EXISTING DATA RACK TO BE DECOMMISSIONED BY VA. CONTRACTOR SHALL COORDINATE WITH VA AS REQUIRED.
- EXISTING VERTICAL CABLING SLEEVE TO BE PRESERVED. EXISTING FIBER OPTIC AND/OR EXISTING VERTICAL CABLING RELATED TO EXISTING TR RACKS TO BE DEMOLISHED.
- EXISTING EQUIPMENT TO BE DEMOLISHED. ASSOCIATED CABLING SHALL BE DEMOLISHED BACK TO SOURCE.
- PROVIDE TELECOMMUNICATIONS OUTLET WITH PORT QUANTITY SHOWN TO REPLACE EXISTING TELECOMMUNICATIONS OUTLET; EXISTING OUTLET CONDUIT SHALL REMAIN AND BE UTILIZED TO FEED NEW CABLING; REFERENCE SHEET DETAIL '1' ON SHEET TN501 AND THE GENERAL NOTES ON THIS SHEET FOR ADDITIONAL INFORMATION. COORDINATE WITH VA FOR EXACT OUTLET PLACEMENT.


KEY PLAN

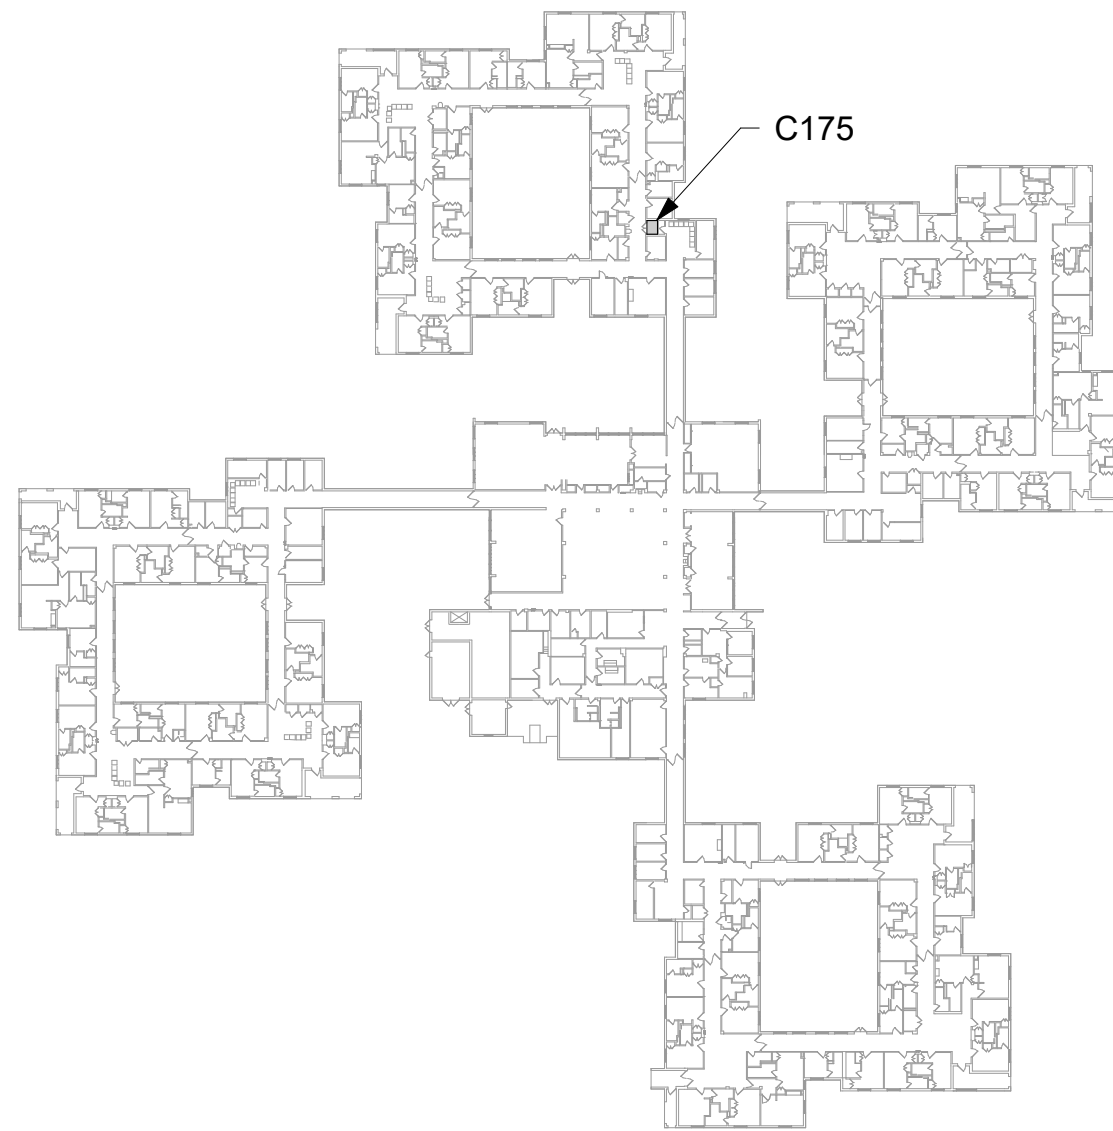


AREA SHOWN

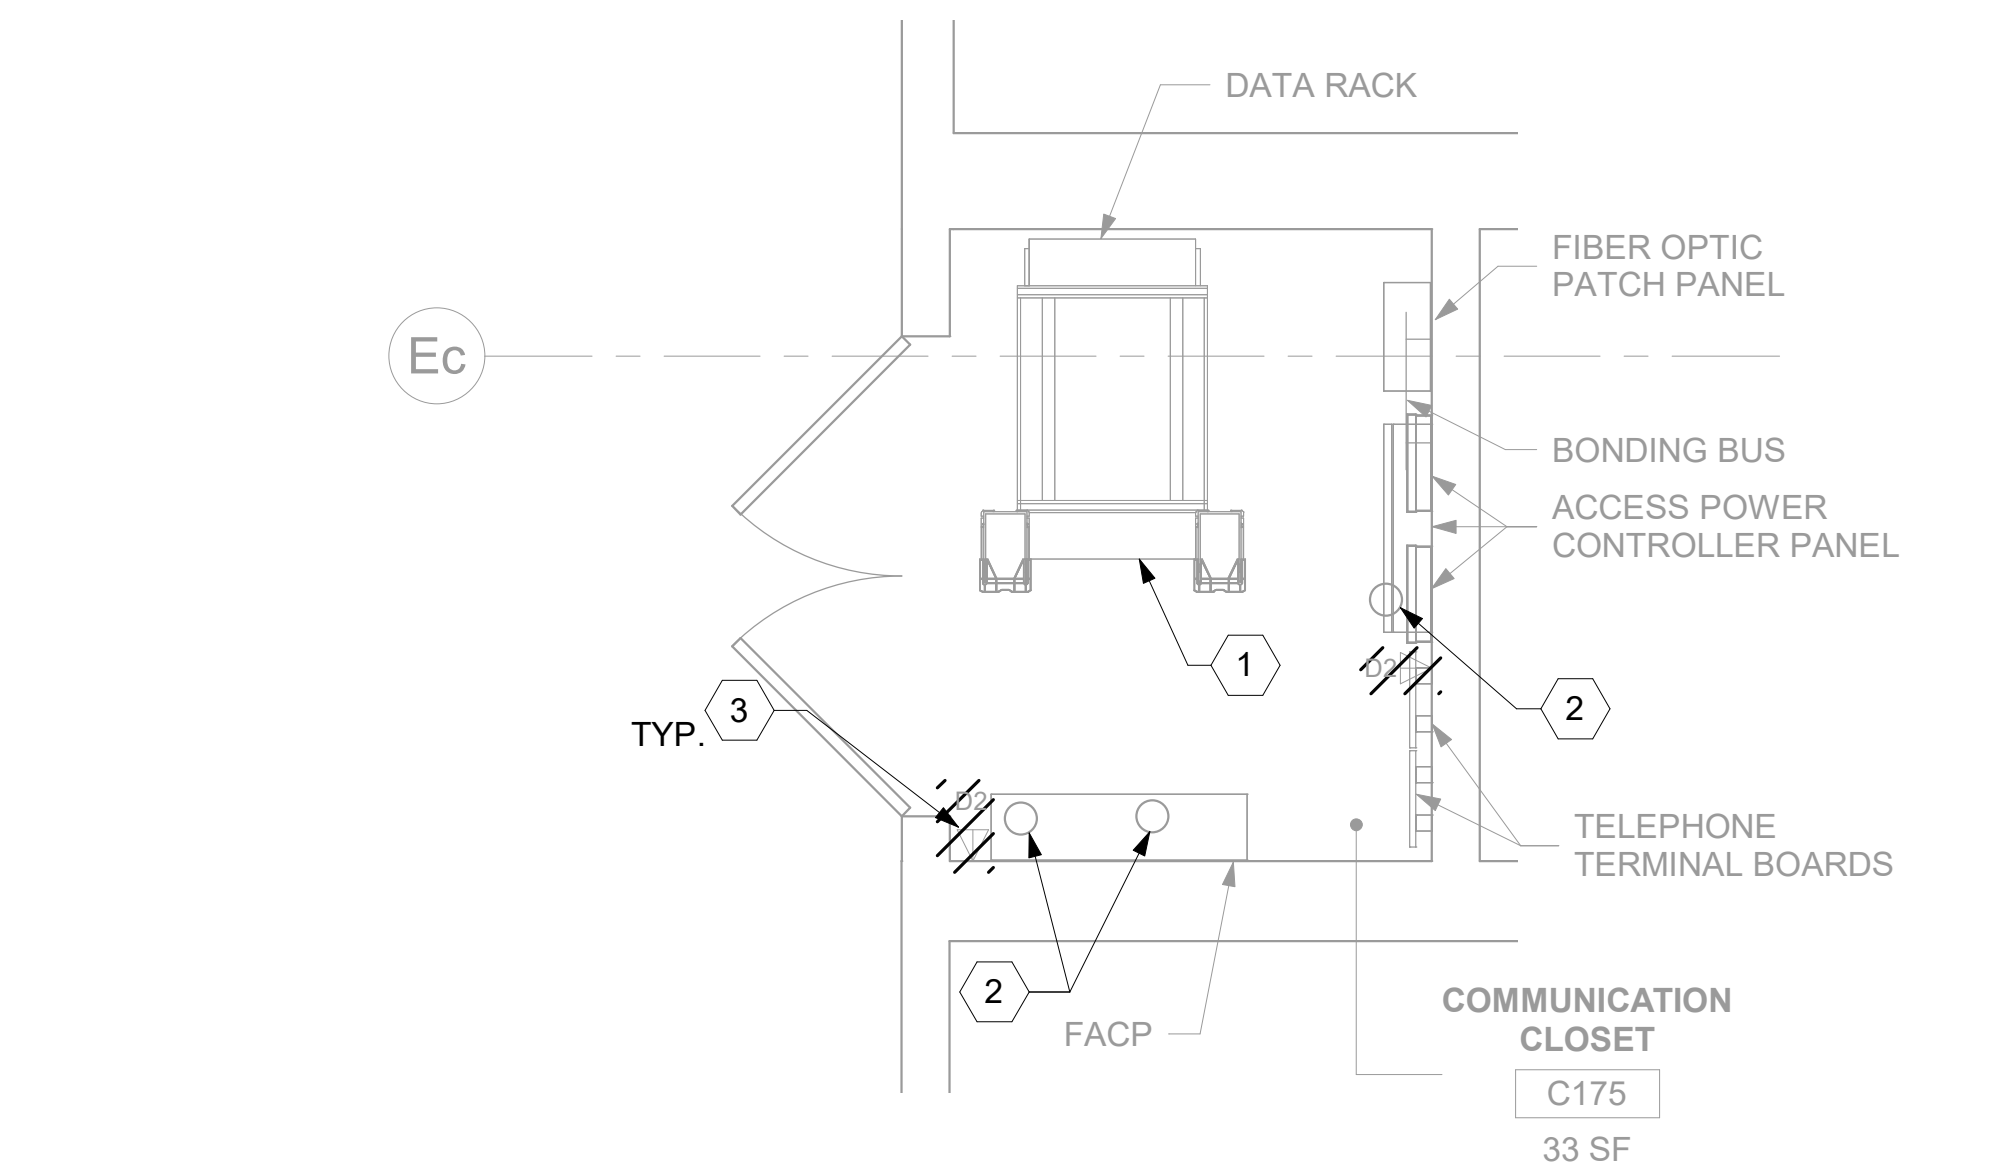


1 RM C175 - DEMOLITION FLOOR PLAN
148TN101A 1/2" = 1'-0"

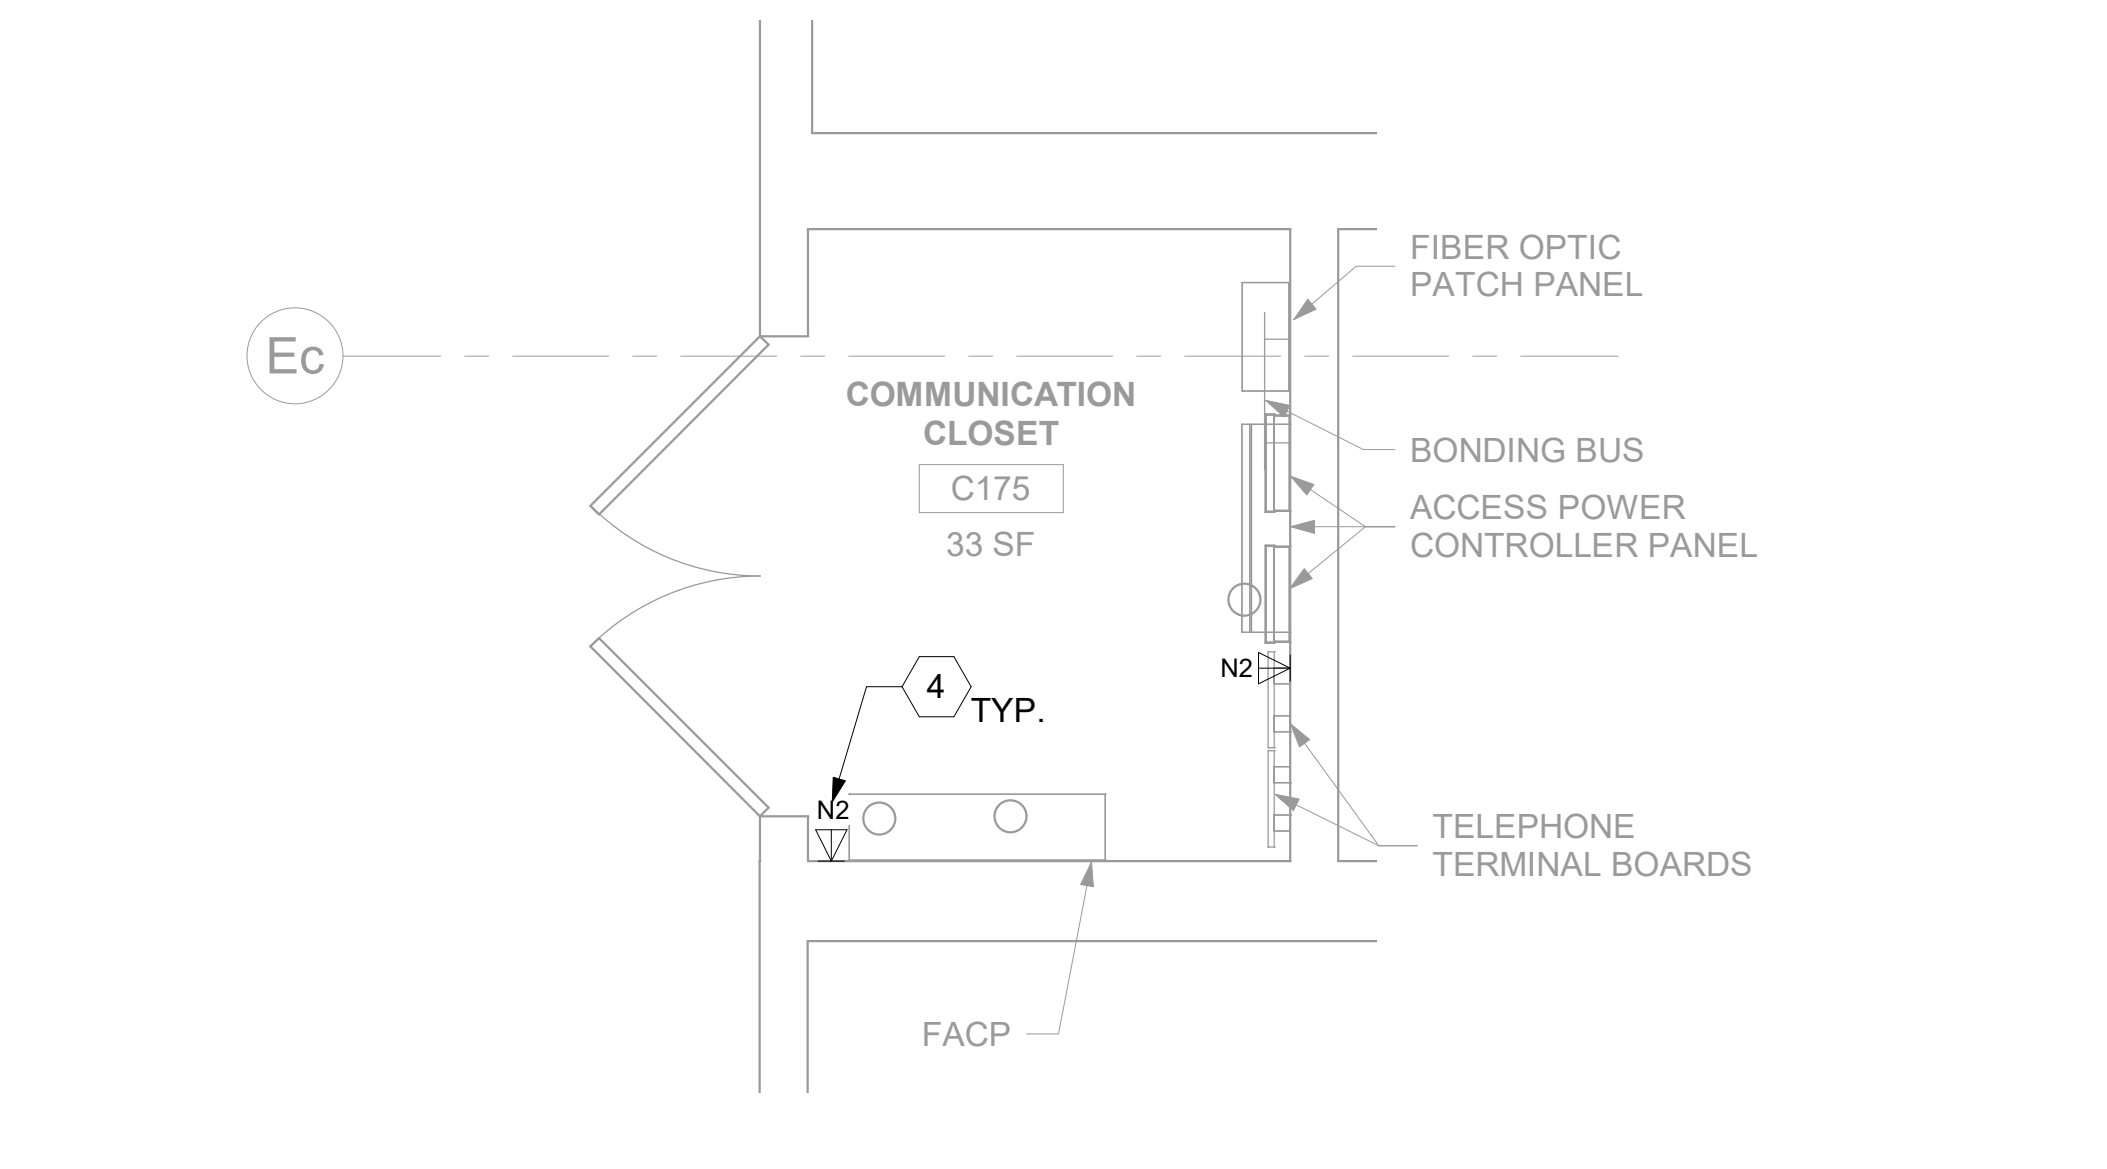

2 RM C175 - TELECOMMUNICATIONS PLAN
148TN101A 1/2" = 1'-0"

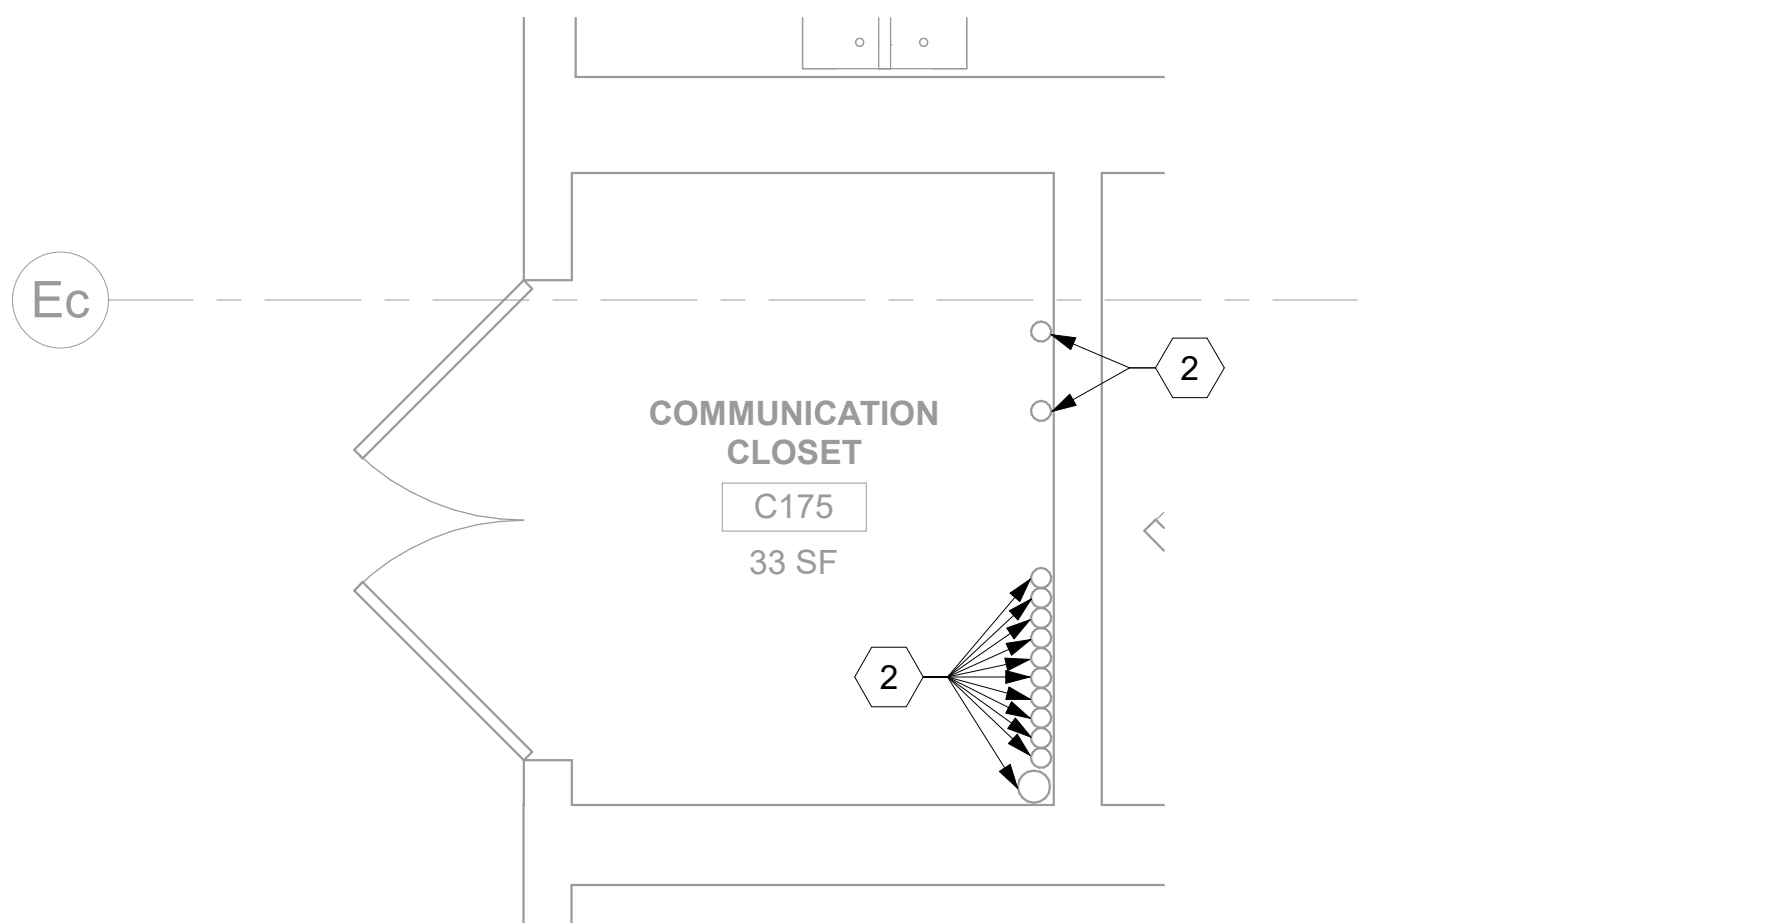

3 RM C175 - DEMOLITION OVERHEAD PLAN
148TN101A 1/2" = 1'-0"

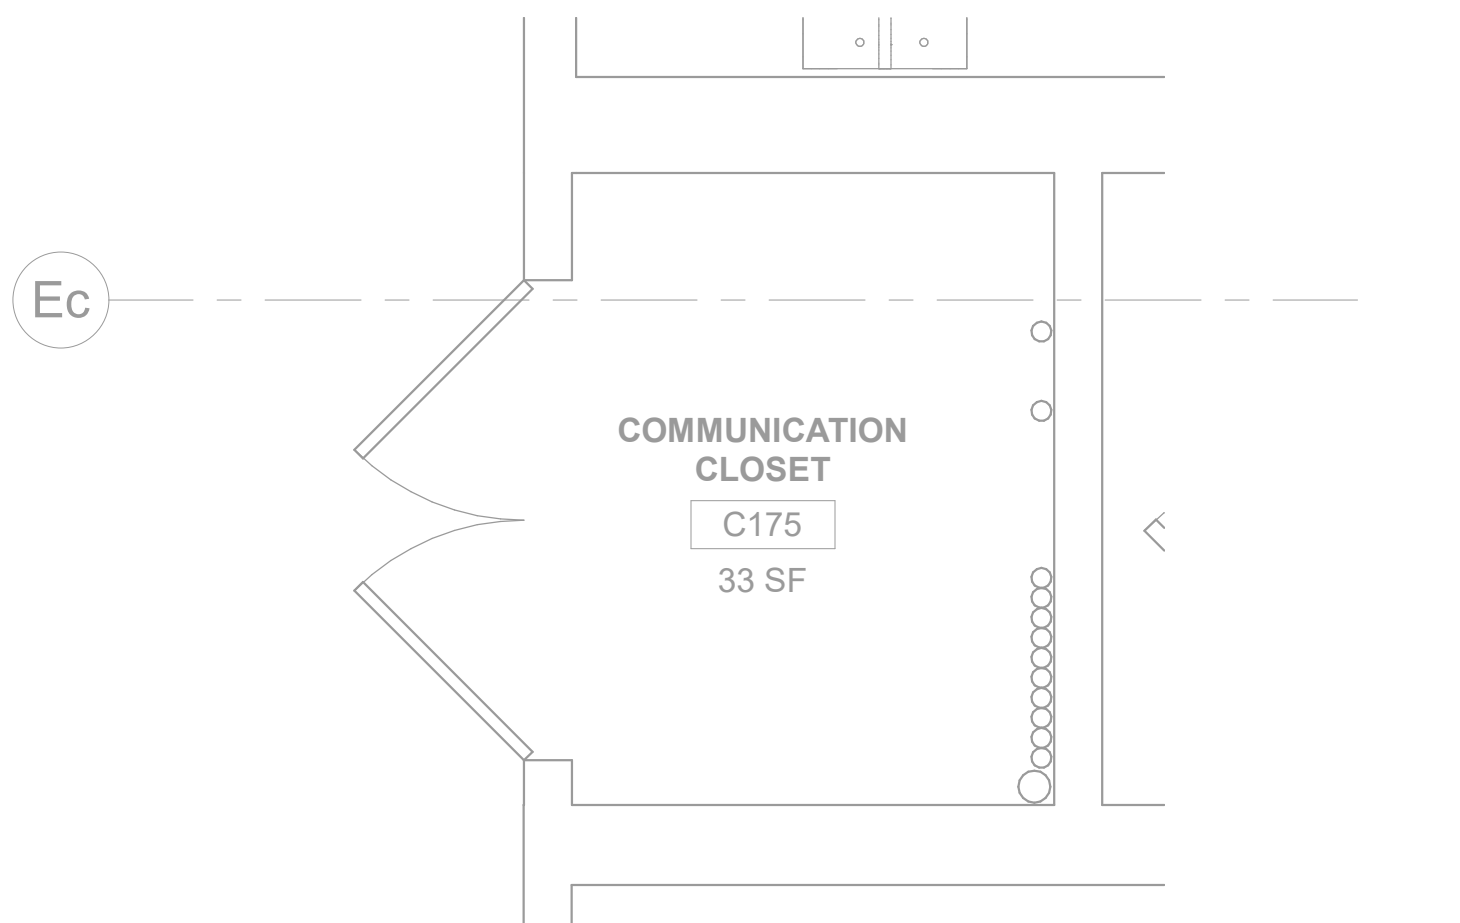

4 RM C175 - OVERHEAD PLAN
148TN101A 1/2" = 1'-0"

Revisions:	Date:

CONSULTANT

ENGINEERING DISCIPLINE:

ARCHITECT/ENGINEER OF RECORD

A/E:
SPEES DESIGN BUILD
23830 PACIFIC HIGHWAY S. SUITE 203
KENT, WA 98032



STAMP



Office of
Construction
and Facilities
Management



U.S. Department
of Veterans Affairs

Drawing Title

BLDG 148 - LEVEL 01 - ENLARGED
TELECOMMUNICATIONS PLANS

Approved:

Phase

100% CONSTRUCTION
DOCUMENTS

FULLY SPRINKLERED

Project Title

EHRM INFRASTRUCTURE
UPGRADES - HAMPTON

Location

HAMPTON VA MEDICAL CENTER, HAMPTON, VIRGINIA

Issue Date

07/18/2025

Checked

KG

Drawn

BCL/GPB

Project Number

590-22-700

Building Number

148

Drawing Number

148TN401g

611 of 713

BM 360/599-22-700
Washington EHRMEE - BLDG
148/11

15/07/2025 11:11:24 am

VA FORM 08 - 6231

12


GENERAL NOTES

- PROTECT ALL EXISTING WORK FROM DAMAGE DURING CONSTRUCTION. ANY DAMAGED MATERIALS, SYSTEMS, COMPONENTS, FINISHES AND THE LIKE, SHALL BE REPAIRED OR REPLACED AT THE EXPENSE OF THE CONTRACTOR TO THE ACCEPTANCE OF THE OWNER.
- SEAL ALL INTERIOR WALL AND CEILING PENETRATIONS TO MATCH EXISTING FIRE RATING OR NEW FIRE RATING, IF REQUIRED. COORDINATE WITH ARCHITECTURAL DRAWINGS AS REQUIRED.
- ALL TELECOMMUNICATIONS CABLING CATEGORY 6 AND BELOW SHALL BE REMOVED AND REPLACED WITH CAT6A PORTS AND CABLE QUANTITIES INDICATED, UNLESS NOTED OTHERWISE.
- TELECOMMUNICATIONS CABLES SHALL BE ROUTED IN EXISTING PATHWAY VACATED BY EXISTING CABLING. PROVIDE RACEWAYS TO EXTEND TO ASSOCIATED TR.
- A TELECOMMUNICATIONS OUTLET UPGRADE SHALL INCLUDE, BUT IS NOT LIMITED TO REMOVING AND DISPOSING EXISTING DEVICES AND CABLES; PROVIDING ALL LABOR, MATERIALS, TOOLS, TEST INSTRUMENTS, AND CONSUMABLES REQUIRED FOR THE INSTALLATION, TERMINATION, TESTING, LABELING, AND CERTIFICATION OF A FULLY FUNCTIONAL CATEGORY 6A OUTLET WITH THE PORT QUANTITY INDICATED.
- WHERE NEW DATA OUTLETS ARE BEING PROVIDED AND EXISTING DATA OUTLET CURRENTLY DOES NOT EXIST, PROVIDE (1) 1" CONDUIT FROM NEW BACKBOX TO ACCESSIBLE CEILING SPACE TO SECURELY ROUTE DATA CABLING FROM OUTLET TO TR VIA CABLE TRAY. IF CABLE TRAY IS NON-EXISTENT, EXTEND RACEWAY FROM OUTLET TO TR AS REQUIRED.
- PROVIDE CONDUITS AND SLEEVES AS REQUIRED FOR ROUTING AND INSTALLATION OF HORIZONTAL AND BACKBONE CABLING. PROVIDE FIRE-STOP MATERIALS TO SEAL IN AND AROUND CONDUIT PER CODE. REFER TO ARCHITECTURAL DRAWINGS FOR PARTITION TYPES AND WALL HEIGHTS.
- ALL TELECOMMUNICATION ROOMS SHALL BE PROVIDED WITH FIRE-RATED PLYWOOD BACKBOARDS. REFERENCE EXACT PLACEMENTS WITH ARCHITECTURE DRAWINGS AS REQUIRED.
- ANY LIVE SYSTEMS IN DEMO'D TR'S MUST REMAIN LIVE. CONTRACTOR TO COORDINATE WITH THE STATION TO IDENTIFY SYSTEMS THAT ARE LIVE. IF SYSTEMS ARE LIVE; INSTALL NEW CABLE FROM DEMO'D TR TO NEW TR. REFER TO DETAIL '3' ON TN506.


KEY NOTES

- EXISTING DATA RACK TO BE DECOMMISSIONED BY VA. CONTRACTOR SHALL COORDINATE WITH VA AS REQUIRED.
- EXISTING VERTICAL CABLING SLEEVE TO BE PRESERVED. EXISTING FIBER OPTIC AND/OR EXISTING VERTICAL CABLING RELATED TO EXISTING TR RACKS TO BE DEMOLISHED.


KEY PLAN

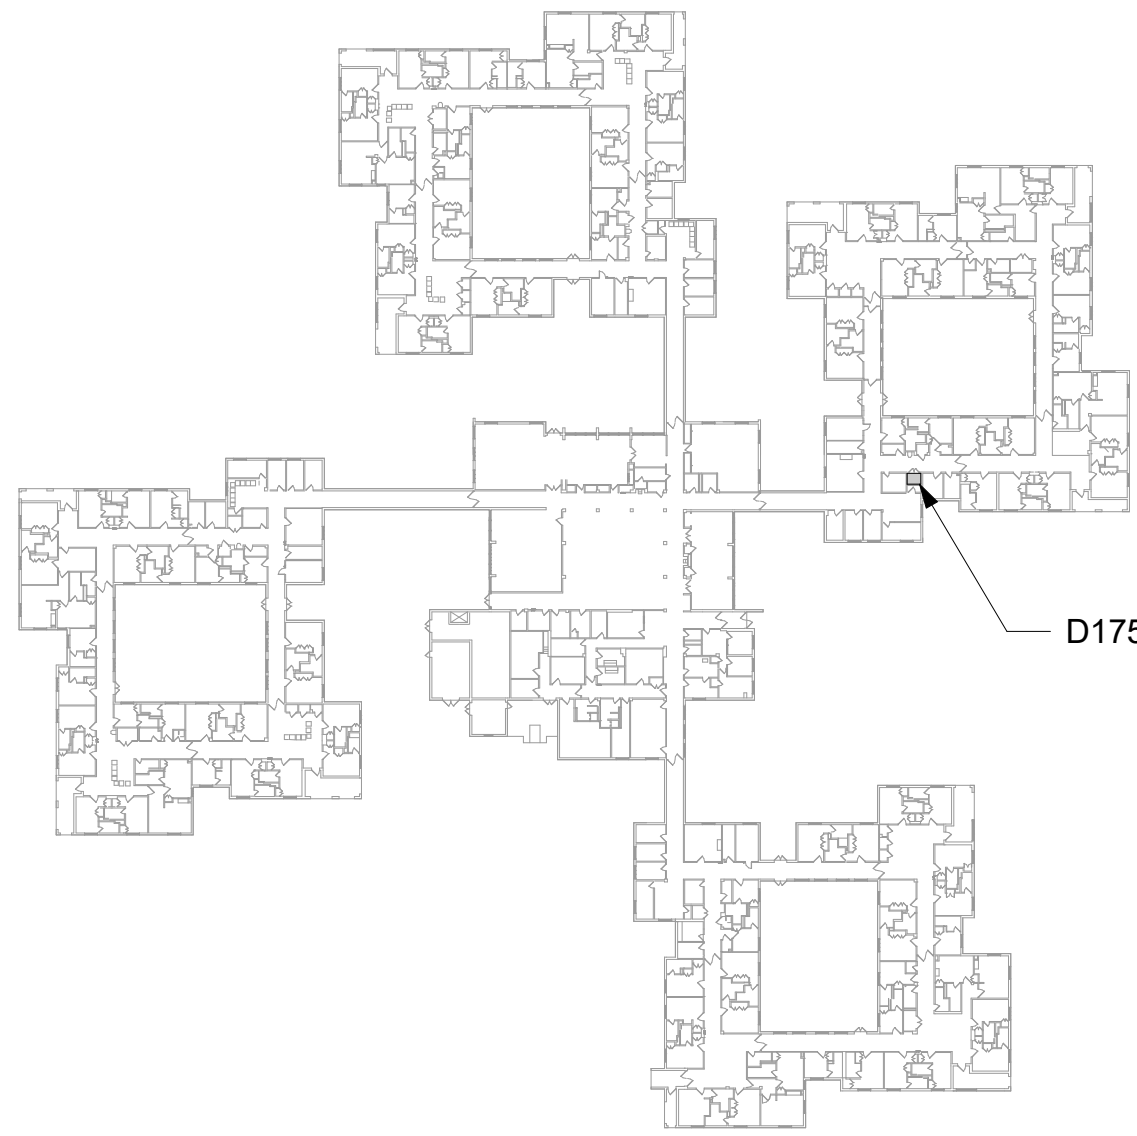


AREA SHOWN

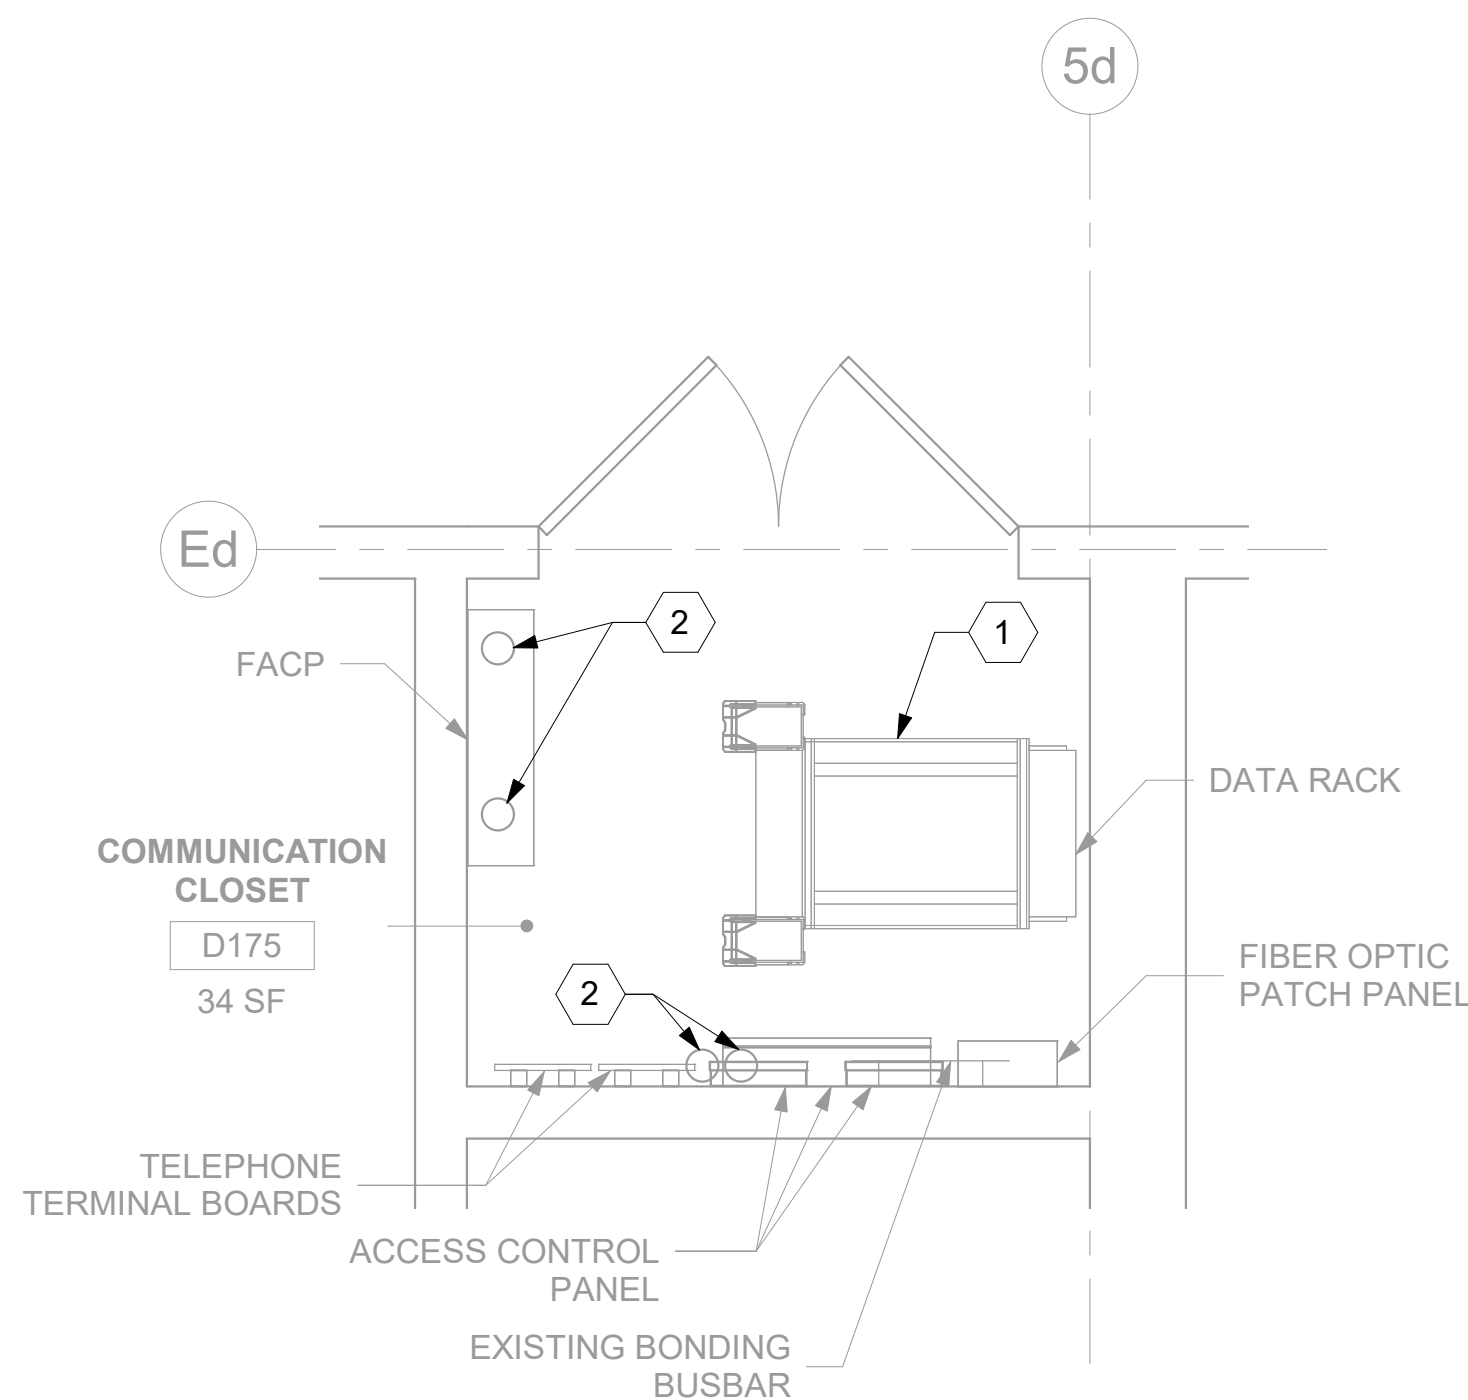


1 RM D175 - DEMOLITION FLOOR PLAN
148TN101A 1/2" = 1'-0"

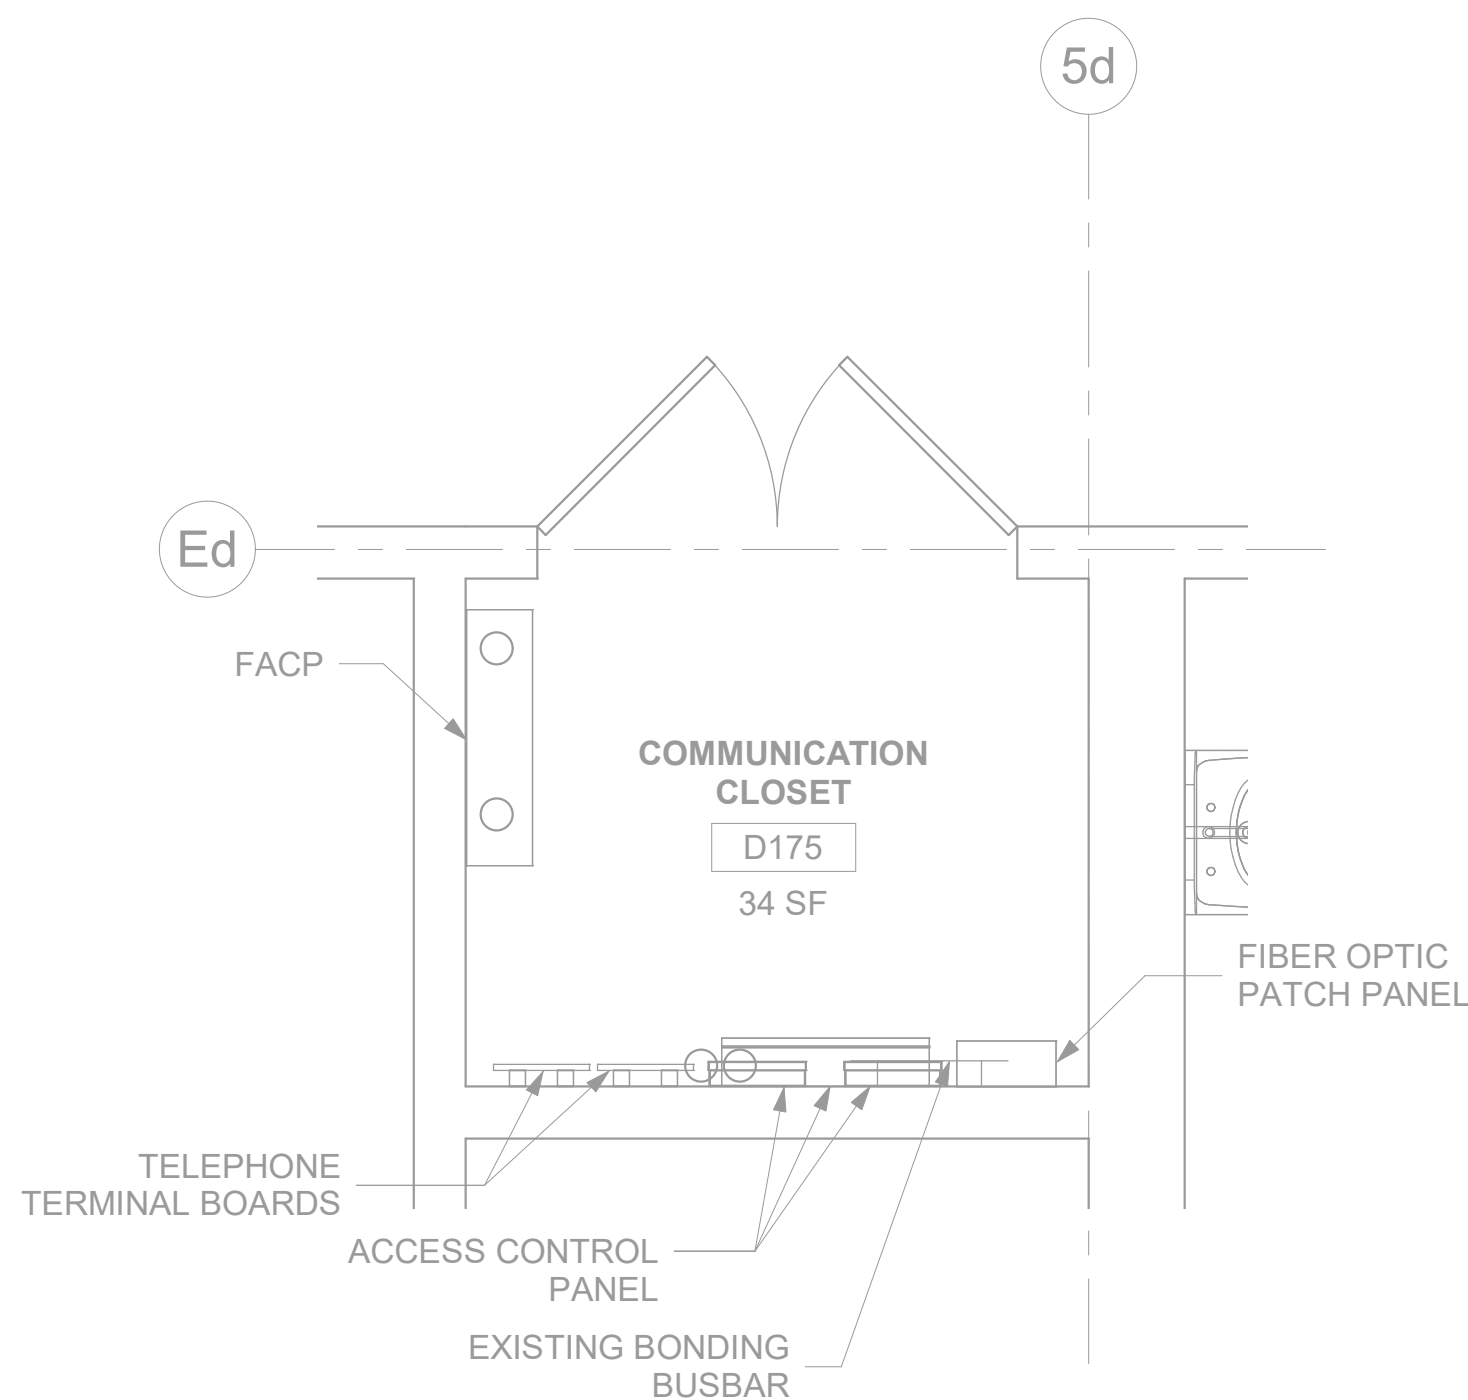

2 RM D175 - TELECOMMUNICATIONS PLAN
148TN101A 1/2" = 1'-0"

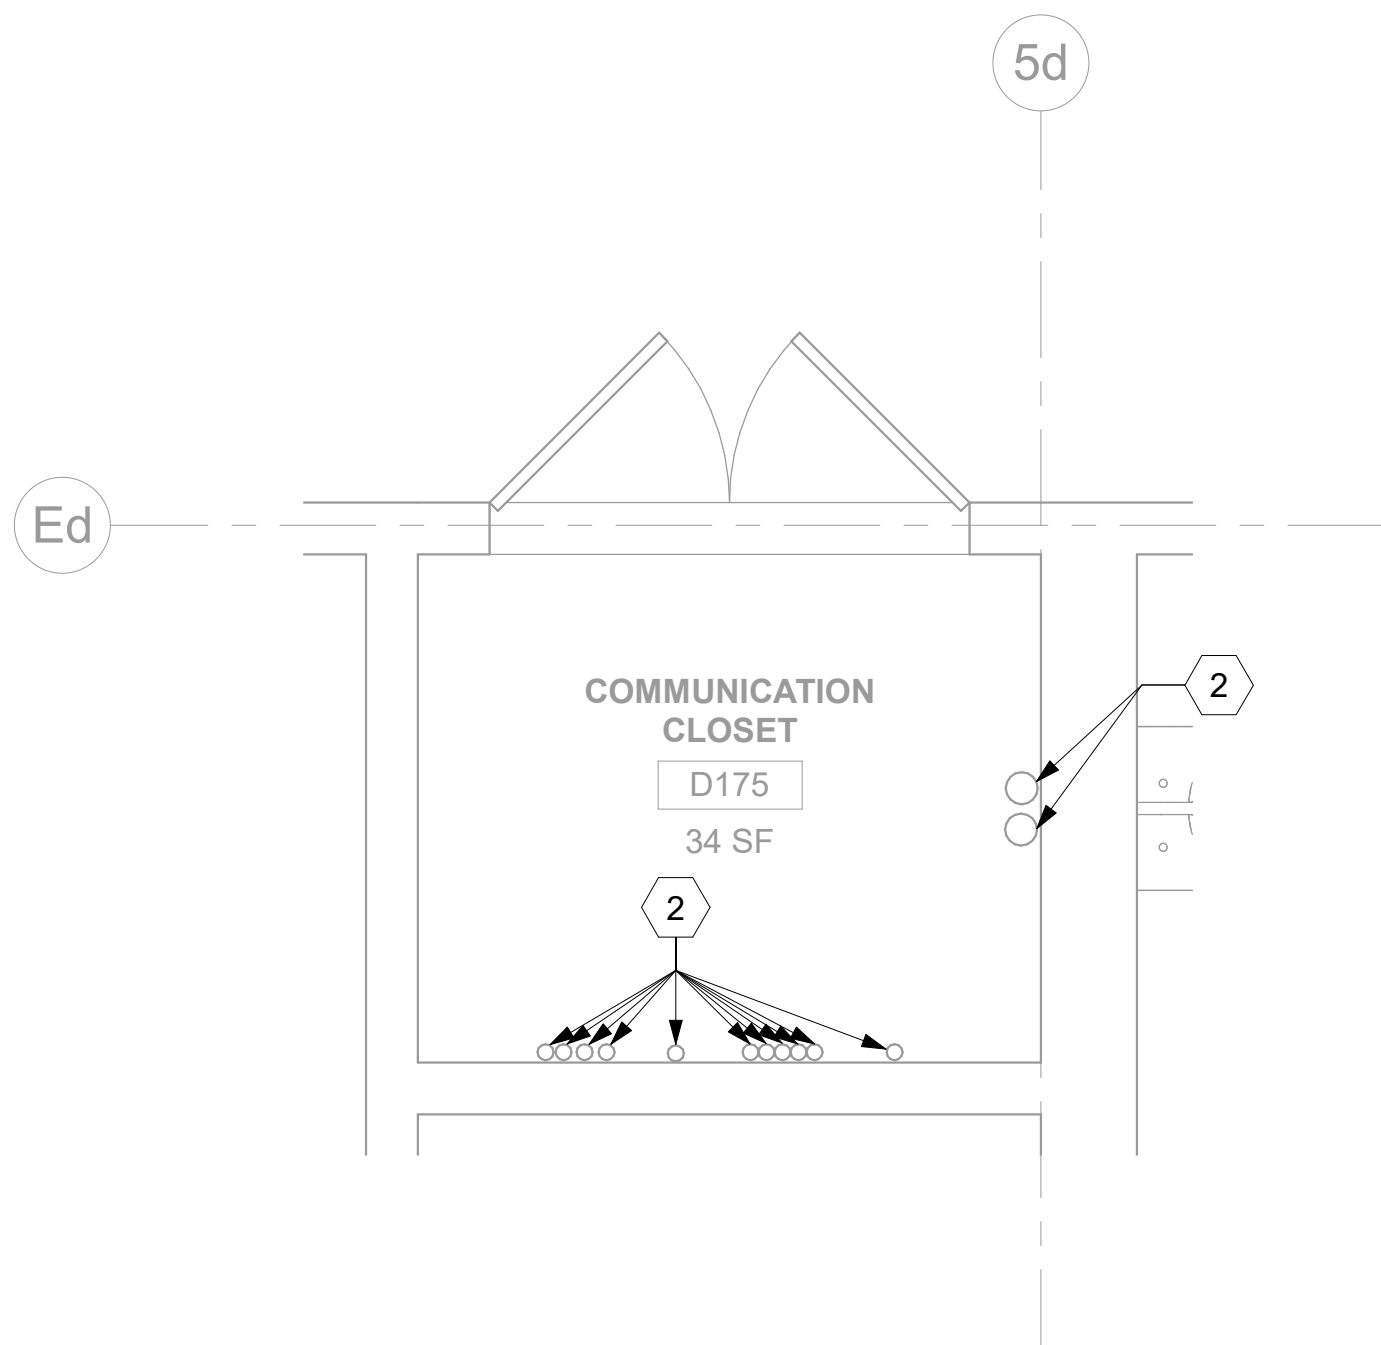

3 RM D175 - DEMOLITION OVERHEAD PLAN
148TN101A 1/2" = 1'-0"

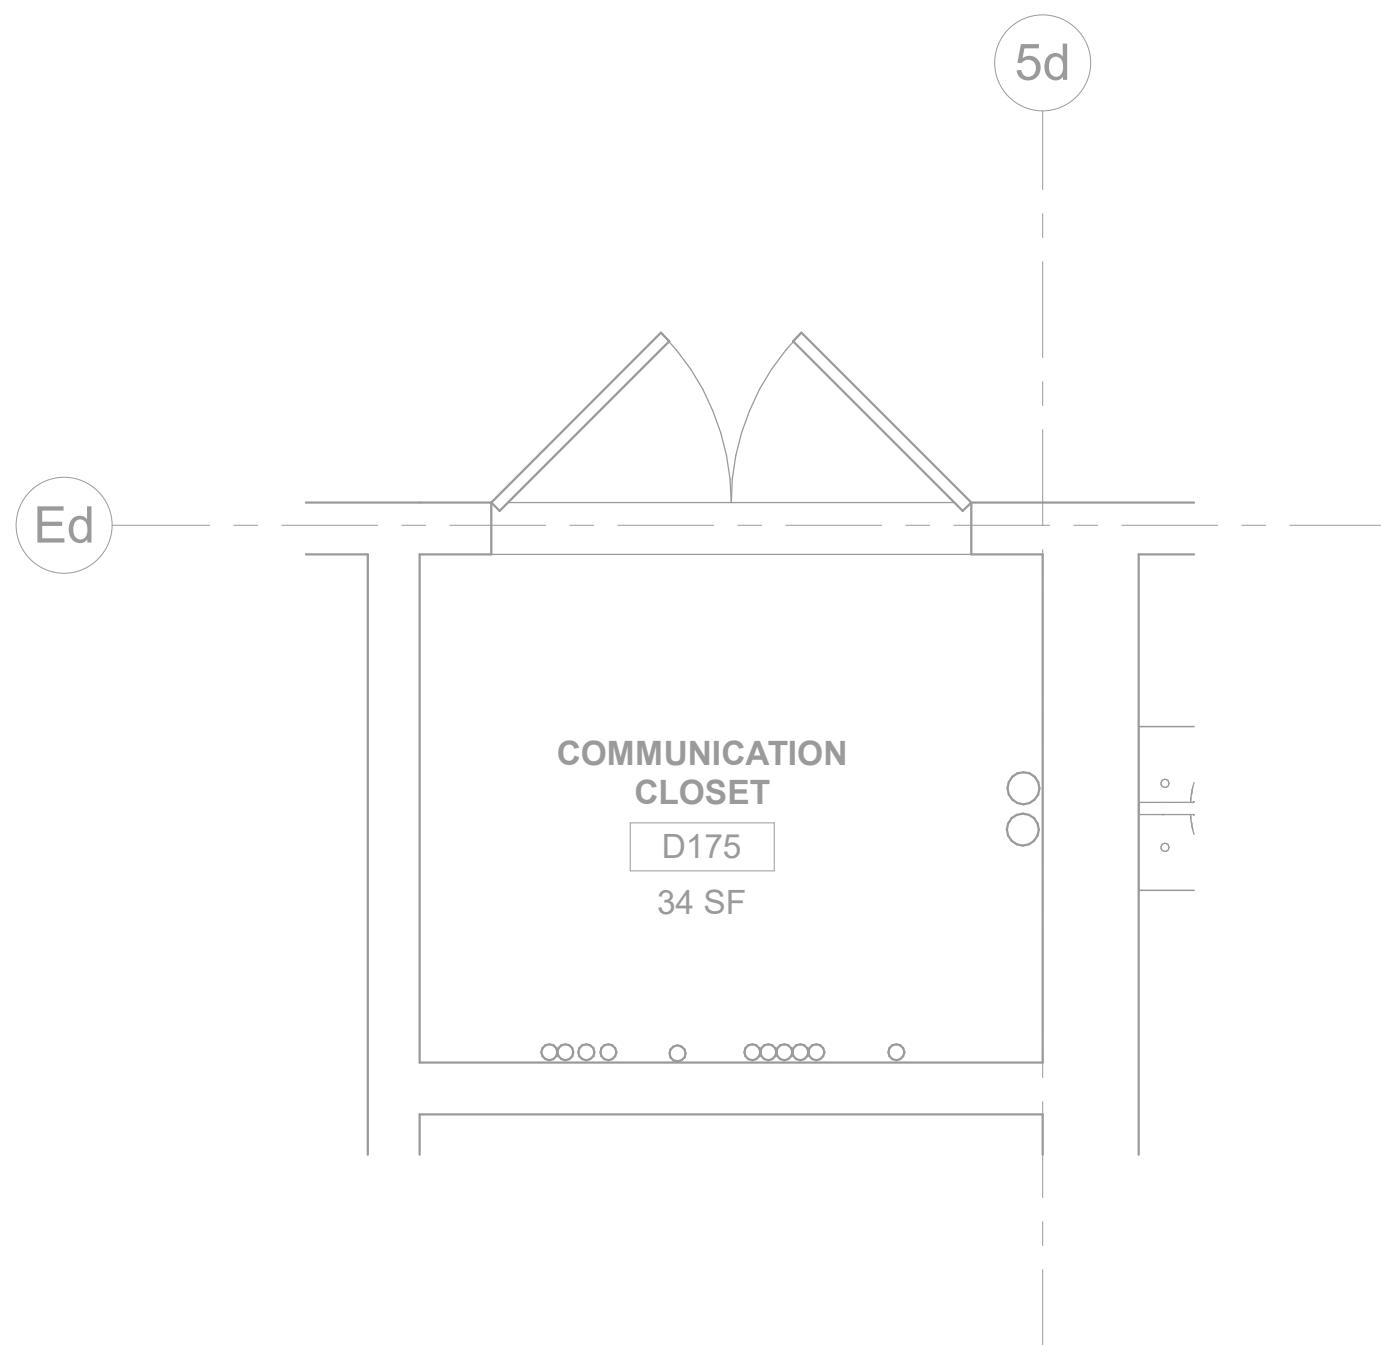

4 RM D175 - OVERHEAD PLAN
148TN101A 1/2" = 1'-0"

CONSULTANT

ENGINEERING DISCIPLINE:

ARCHITECT/ENGINEER OF RECORD

A/E:
SPEES DESIGN BUILD
23830 PACIFIC HIGHWAY S. SUITE 203
KENT, WA 98032



STAMP



Office of
Construction
and Facilities
Management



U.S. Department
of Veterans Affairs

Drawing Title

BLDG 148 - LEVEL 01 - ENLARGED
TELECOMMUNICATIONS PLANS

Approved:

Phase

100% CONSTRUCTION
DOCUMENTS

FULLY SPRINKLERED

Project Title

EHRM INFRASTRUCTURE
UPGRADES - HAMPTON

Location

HAMPTON VA MEDICAL CENTER, HAMPTON, VIRGINIA

Issue Date

07/18/2025

Checked

KG

Drawn

BCL/GPB

Project Number

590-22-700

Building Number

148

Drawing Number

148TN401h

612 of 713

BM 360/599-22-700
Washington EHRMEE - BLDG
148TN

15/07/2025 11:11:38 am

VA FORM 08 - 6231

CONSULTANT

ENGINEERING DISCIPLINE:

ARCHITECT/ENGINEER OF RECORD

A/E:
SPEES DESIGN BUILD
23830 PACIFIC HIGHWAY S. SUITE 203
KENT, WA 98032



STAMP



Office of
Construction
and Facilities
Management



U.S. Department
of Veterans Affairs

Drawing Title

BLDG 148 - LEVEL 01 - ENLARGED
TELECOMMUNICATIONS PLANS

Approved:

Phase

100% CONSTRUCTION
DOCUMENTS

FULLY SPRINKLERED

Project Title

EHRM INFRASTRUCTURE
UPGRADES - HAMPTON

Location

HAMPTON VA MEDICAL CENTER, HAMPTON, VIRGINIA

Issue Date

07/18/2025

Checked

KG

Drawn

BCL/GPB

Project Number

590-22-700

Building Number

148

Drawing Number

148TN401i

613 of 713


GENERAL NOTES

- PROTECT ALL EXISTING WORK FROM DAMAGE DURING CONSTRUCTION. ANY DAMAGED MATERIALS, SYSTEMS, COMPONENTS, FINISHES AND THE LIKE, SHALL BE REPAIRED OR REPLACED AT THE EXPENSE OF THE CONTRACTOR TO THE ACCEPTANCE OF THE OWNER.
- SEAL ALL INTERIOR WALL AND CEILING PENETRATIONS TO MATCH EXISTING FIRE RATING OR NEW FIRE RATING, IF REQUIRED. COORDINATE WITH ARCHITECTURAL DRAWINGS AS REQUIRED.
- ALL TELECOMMUNICATIONS CABLING CATEGORY 6 AND BELOW SHALL BE REMOVED AND REPLACED WITH CAT6A PORTS AND CABLE QUANTITIES INDICATED, UNLESS NOTED OTHERWISE.
- TELECOMMUNICATIONS CABLES SHALL BE ROUTED IN EXISTING PATHWAY VACATED BY EXISTING CABLING. PROVIDE RACEWAYS TO EXTEND TO ASSOCIATED TR.
- A TELECOMMUNICATIONS OUTLET UPGRADE SHALL INCLUDE, BUT IS NOT LIMITED TO REMOVING AND DISPOSING EXISTING DEVICES AND CABLES; PROVIDING ALL LABOR, MATERIALS, TOOLS, TEST INSTRUMENTS, AND CONSUMABLES REQUIRED FOR THE INSTALLATION, TERMINATION, TESTING, LABELING, AND CERTIFICATION OF A FULLY FUNCTIONAL CATEGORY 6A OUTLET WITH THE PORT QUANTITY INDICATED.
- WHERE NEW DATA OUTLETS ARE BEING PROVIDED AND EXISTING DATA OUTLET CURRENTLY DOES NOT EXIST, PROVIDE (1) 1" CONDUIT FROM NEW BACKBOX TO ACCESSIBLE CEILING SPACE TO SECURELY ROUTE DATA CABLING FROM OUTLET TO TR VIA CABLE TRAY. IF CABLE TRAY IS NON-EXISTENT, EXTEND RACEWAY FROM OUTLET TO TR AS REQUIRED.
- PROVIDE CONDUITS AND SLEEVES AS REQUIRED FOR ROUTING AND INSTALLATION OF HORIZONTAL AND BACKBONE CABLING. PROVIDE FIRE-STOP MATERIALS TO SEAL IN AND AROUND CONDUIT PER CODE. REFER TO ARCHITECTURAL DRAWINGS FOR PARTITION TYPES AND WALL HEIGHTS.
- ALL TELECOMMUNICATION ROOMS SHALL BE PROVIDED WITH FIRE-RATED PLYWOOD BACKBOARDS. REFERENCE EXACT PLACEMENTS WITH ARCHITECTURE DRAWINGS AS REQUIRED.
- ANY LIVE SYSTEMS IN DEMO'D TR'S MUST REMAIN LIVE. CONTRACTOR TO COORDINATE WITH THE STATION TO IDENTIFY SYSTEMS THAT ARE LIVE. IF SYSTEMS ARE LIVE; INSTALL NEW CABLE FROM DEMO'D TR TO NEW TR. REFER TO DETAIL '3' ON TN506.


KEY NOTES

- EXISTING DATA RACK TO BE DECOMMISSIONED BY VA. CONTRACTOR SHALL COORDINATE WITH VA AS REQUIRED.
- EXISTING VERTICAL CABLING SLEEVE TO BE PRESERVED. EXISTING FIBER OPTIC AND/OR EXISTING VERTICAL CABLING RELATED TO EXISTING TR RACKS TO BE DEMOLISHED.
- EXISTING WIRELESS ACCESS POINT TO BE RE-FED WITH (2) CAT6A CABLES.
- EXISTING PENETRATIONS WITH CABLING TO BE REMOVED. CONTRACTOR SHALL PATHC AND FIREPROOF OPENINGS. COORDINATE WITH ARCHITECTURAL DRAWINGS AND SPECIFICATIONS.

KEY PLAN

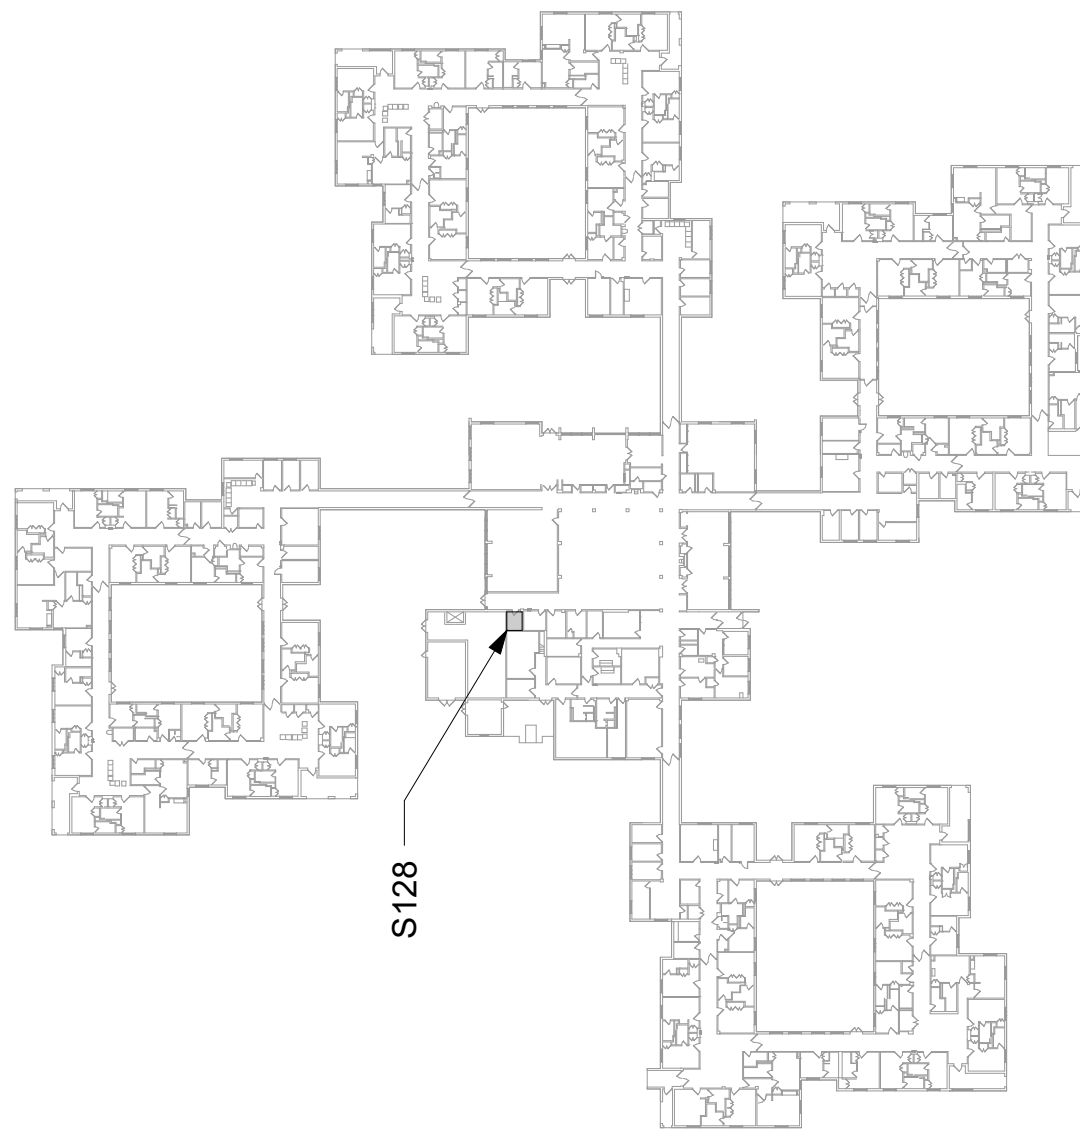


AREA SHOWN

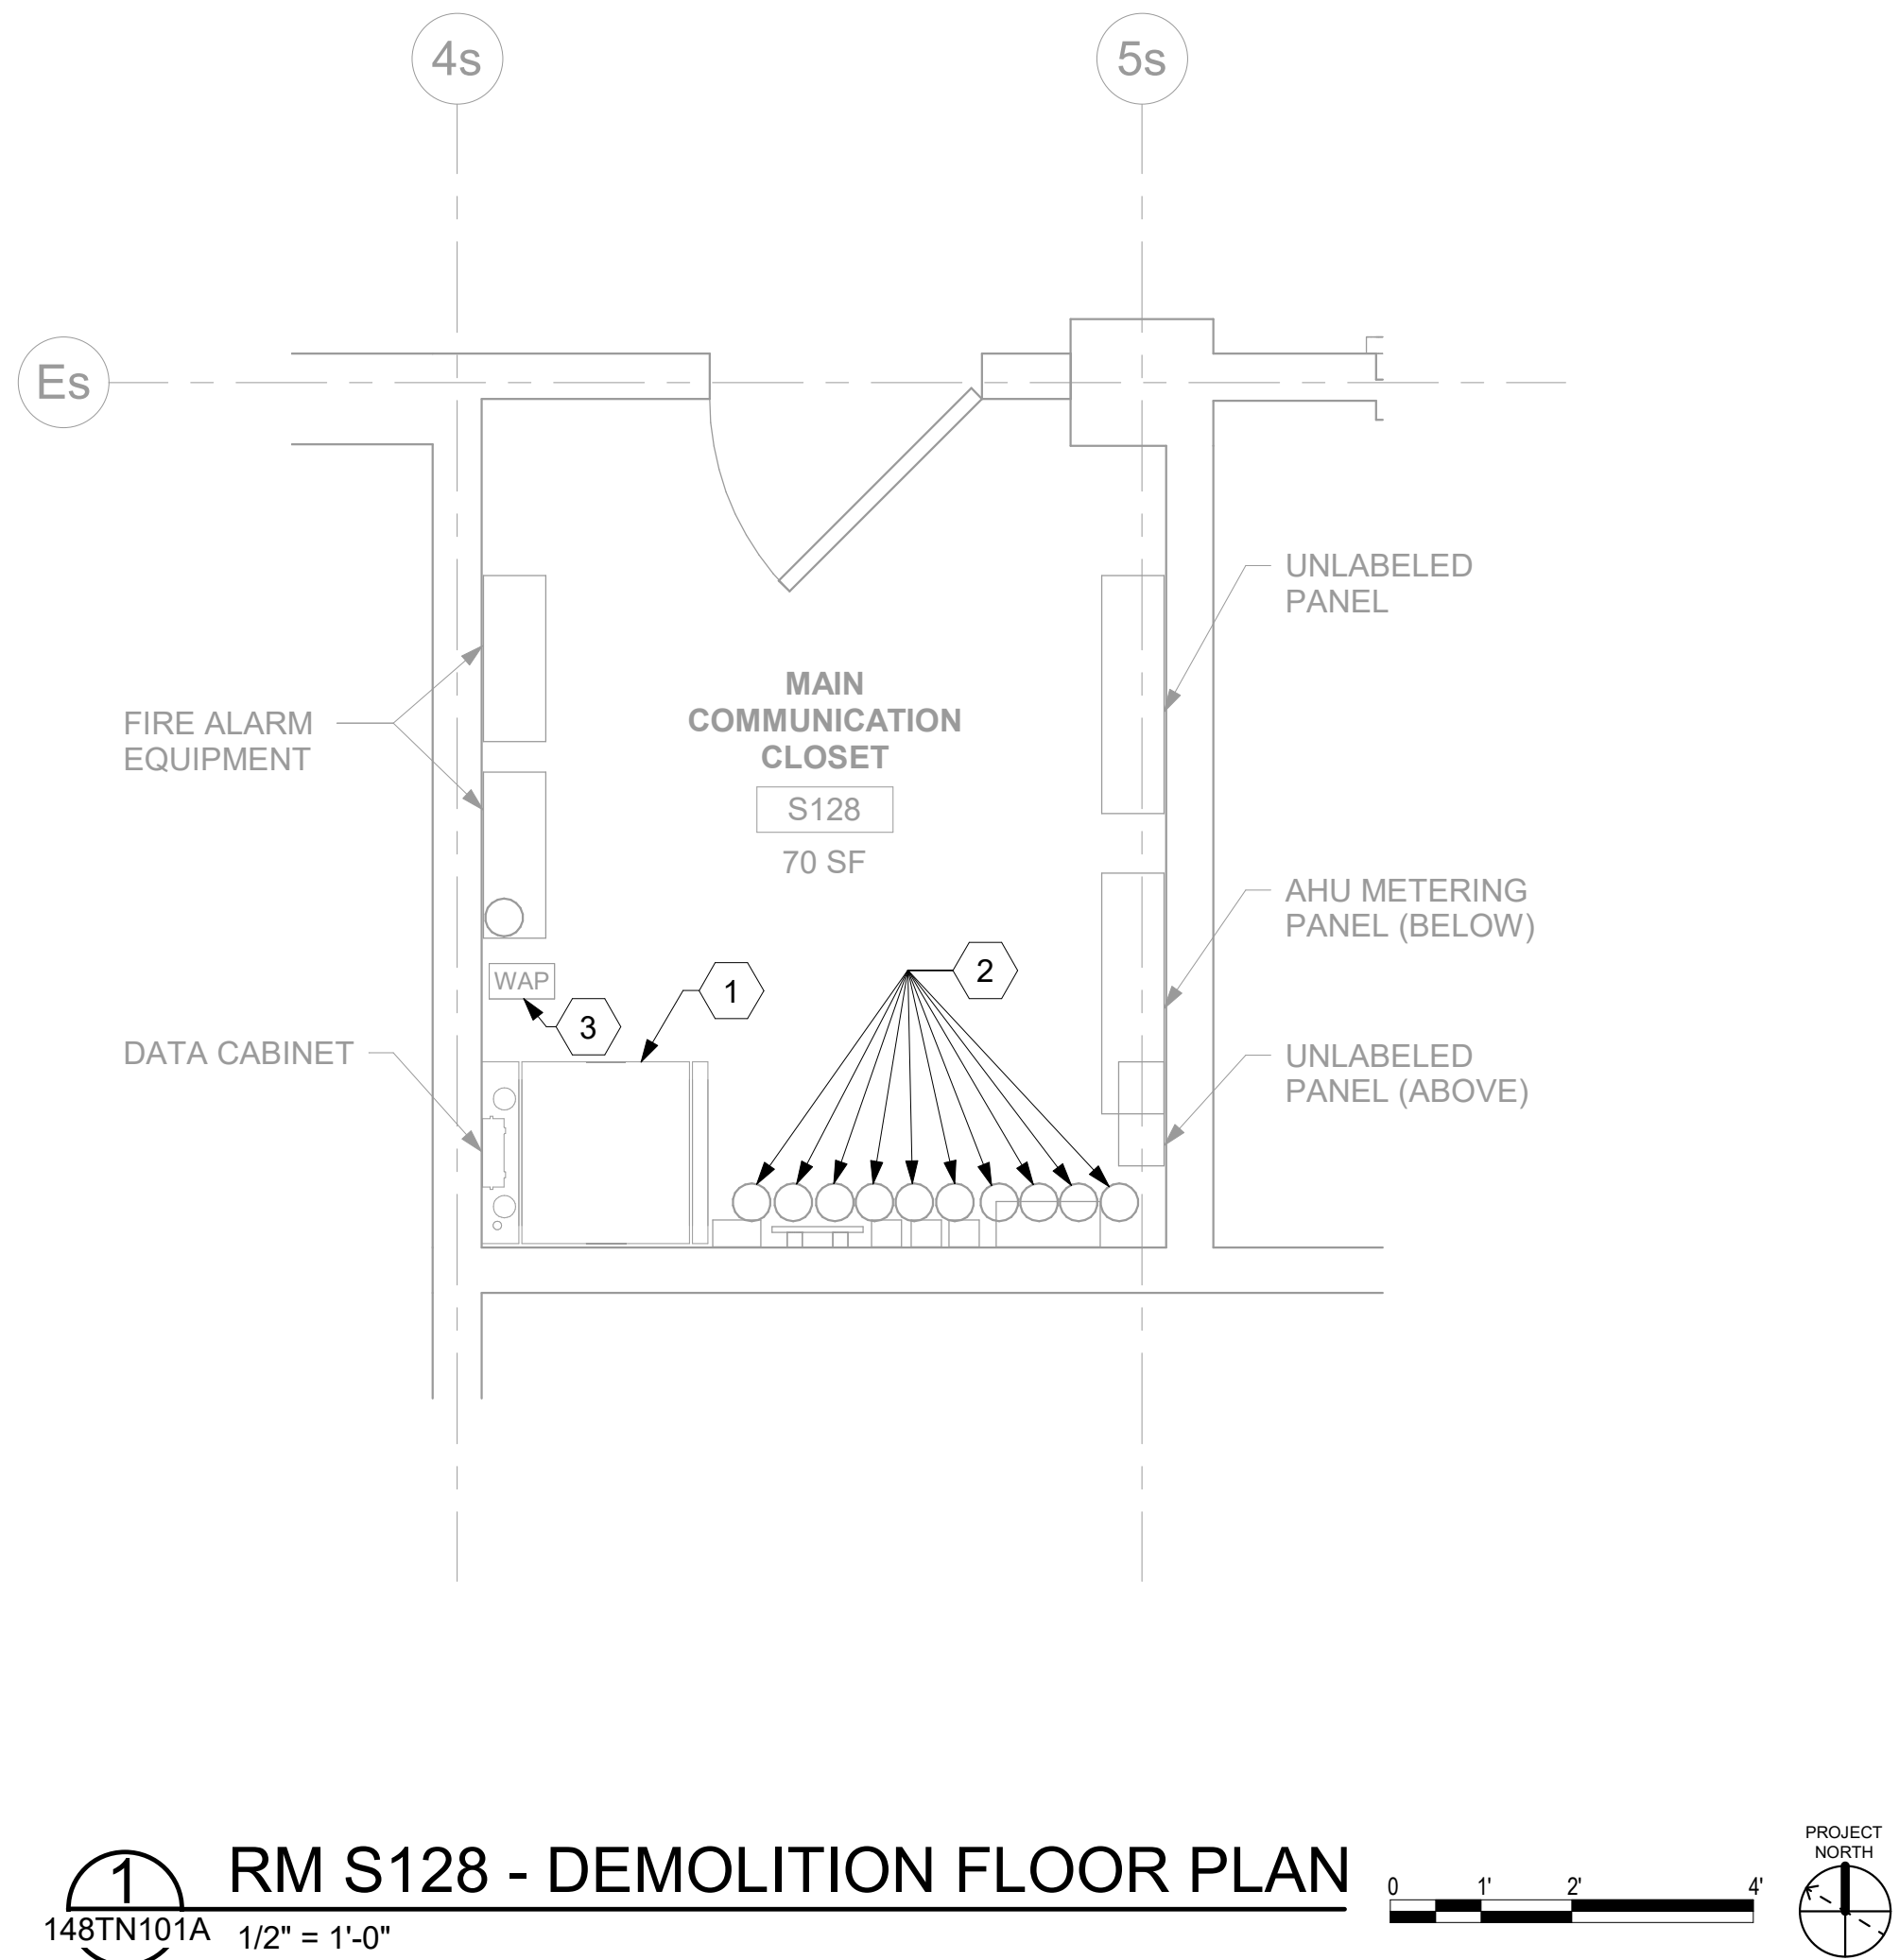


1 RM S128 - DEMOLITION FLOOR PLAN

148TN101A 1/2" = 1'-0"

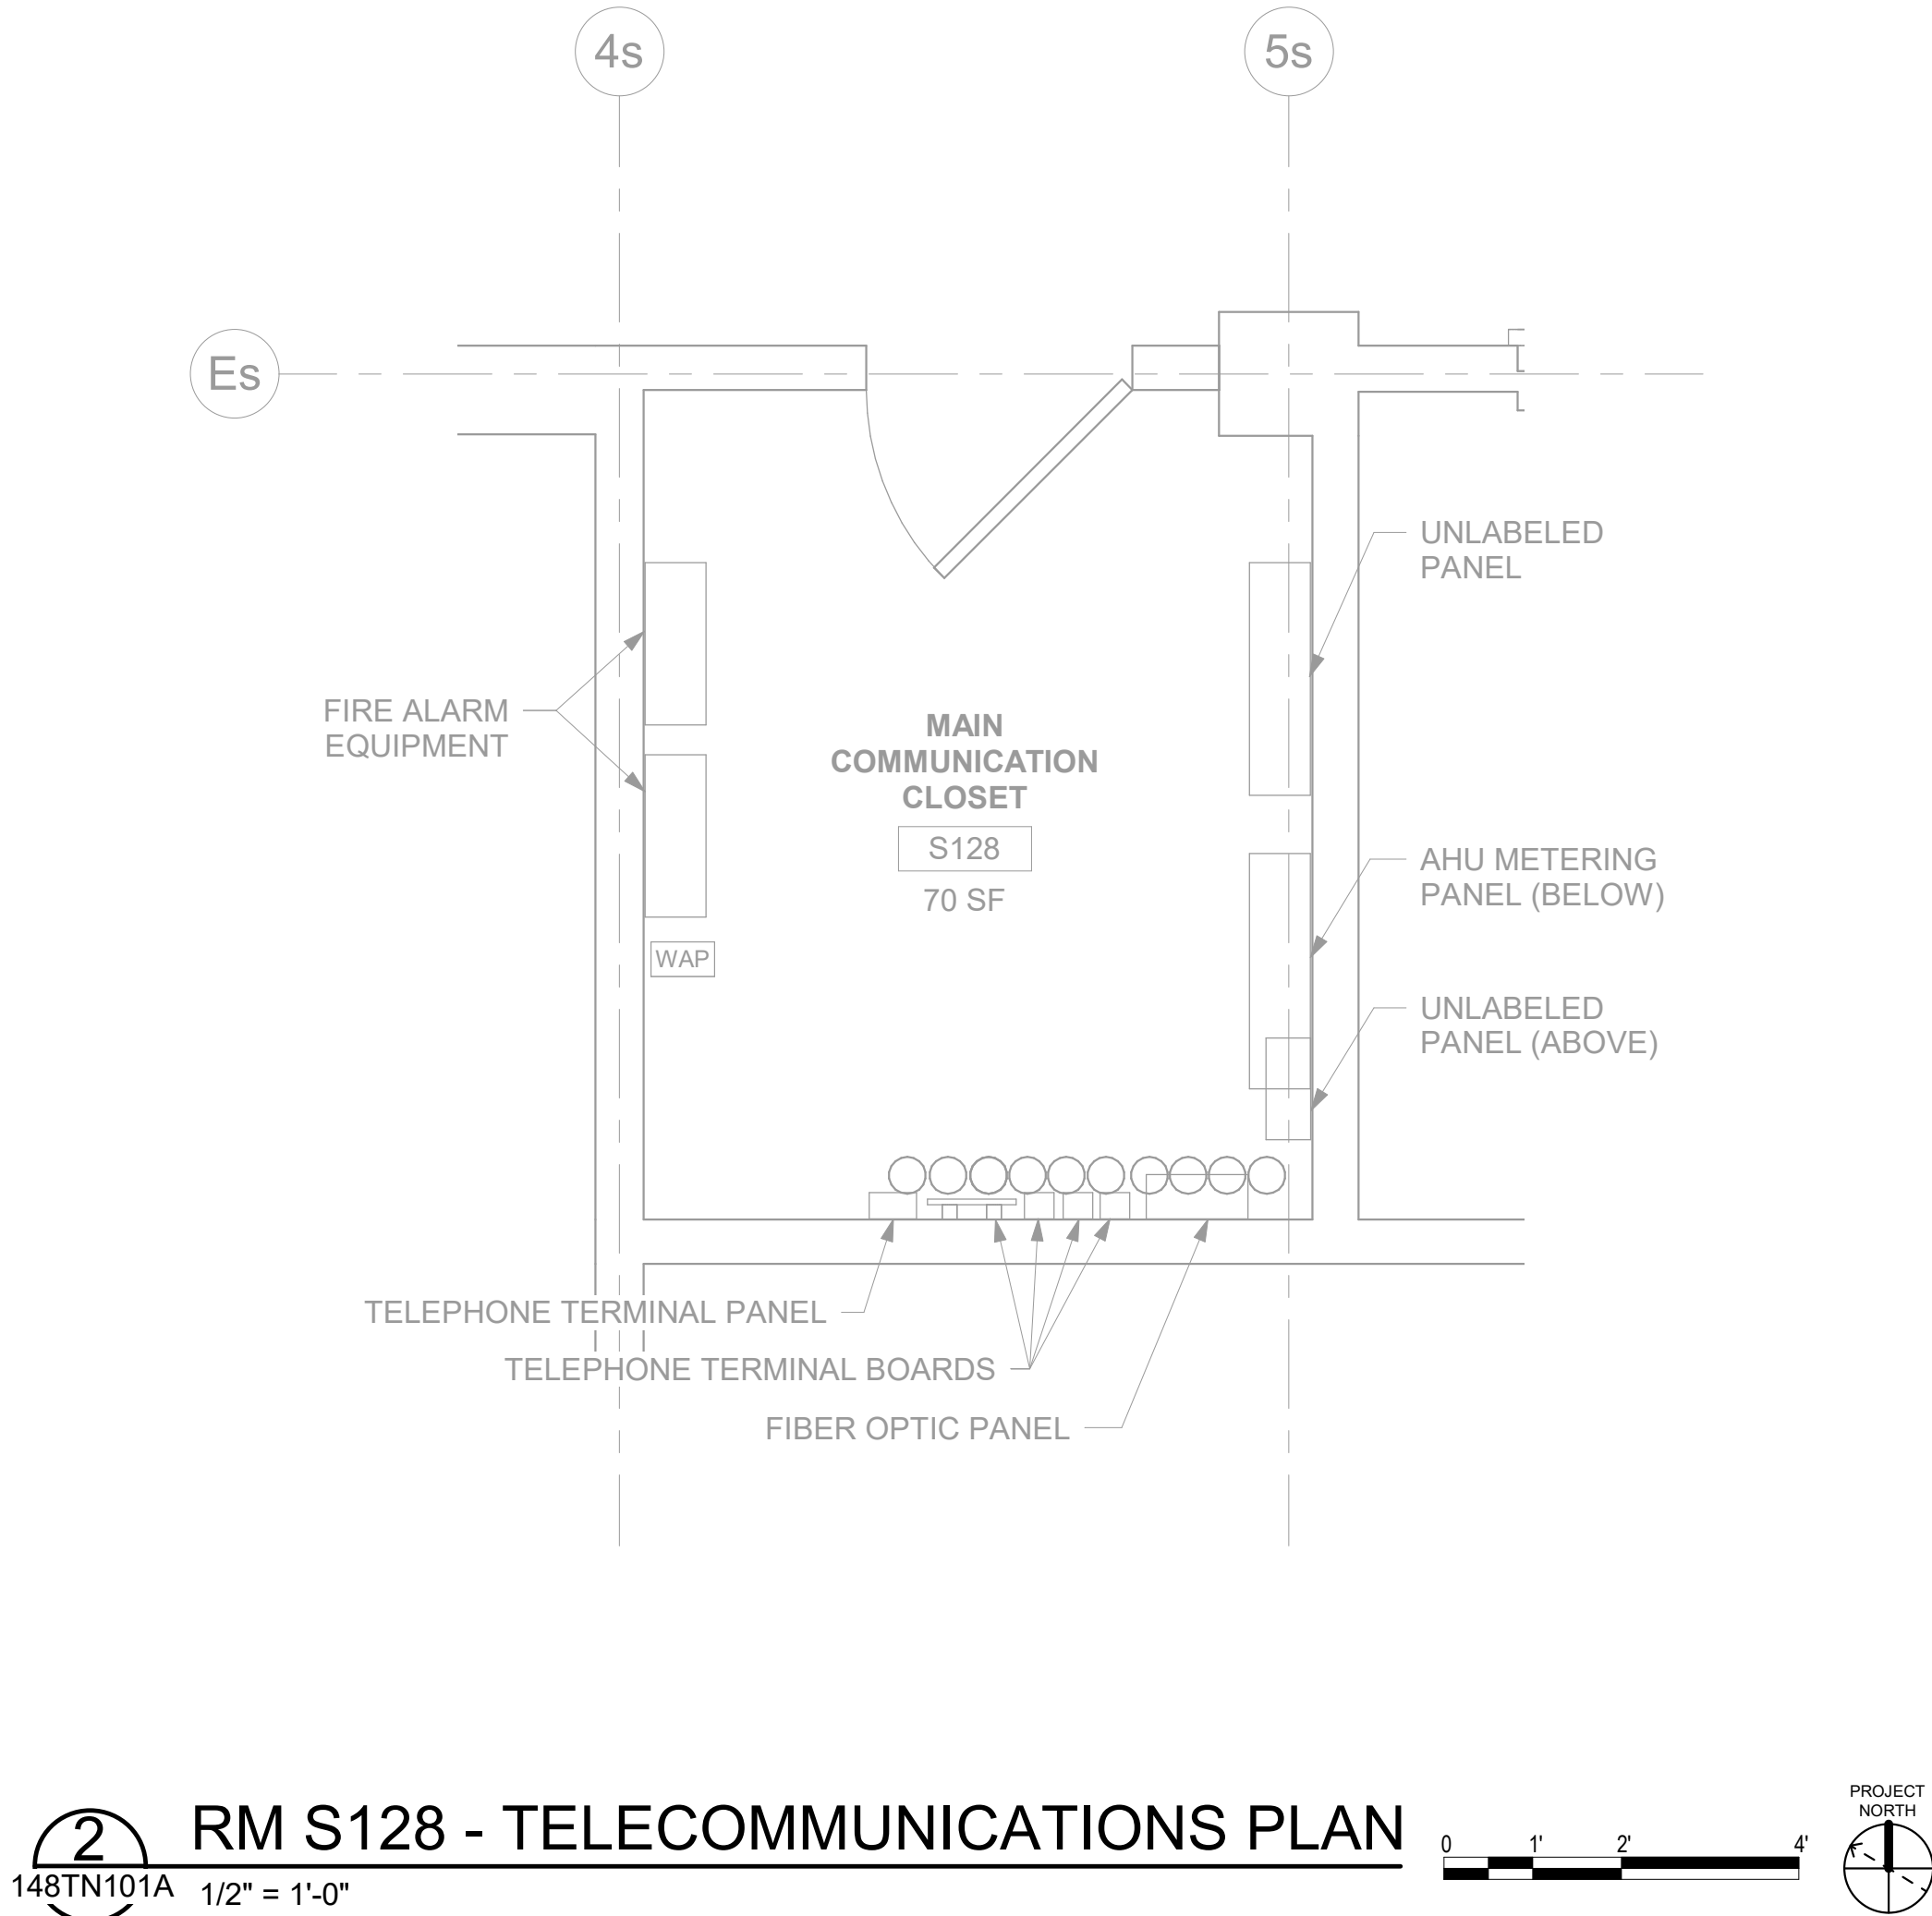


2 RM S128 - TELECOMMUNICATIONS PLAN

148TN101A 1/2" = 1'-0"

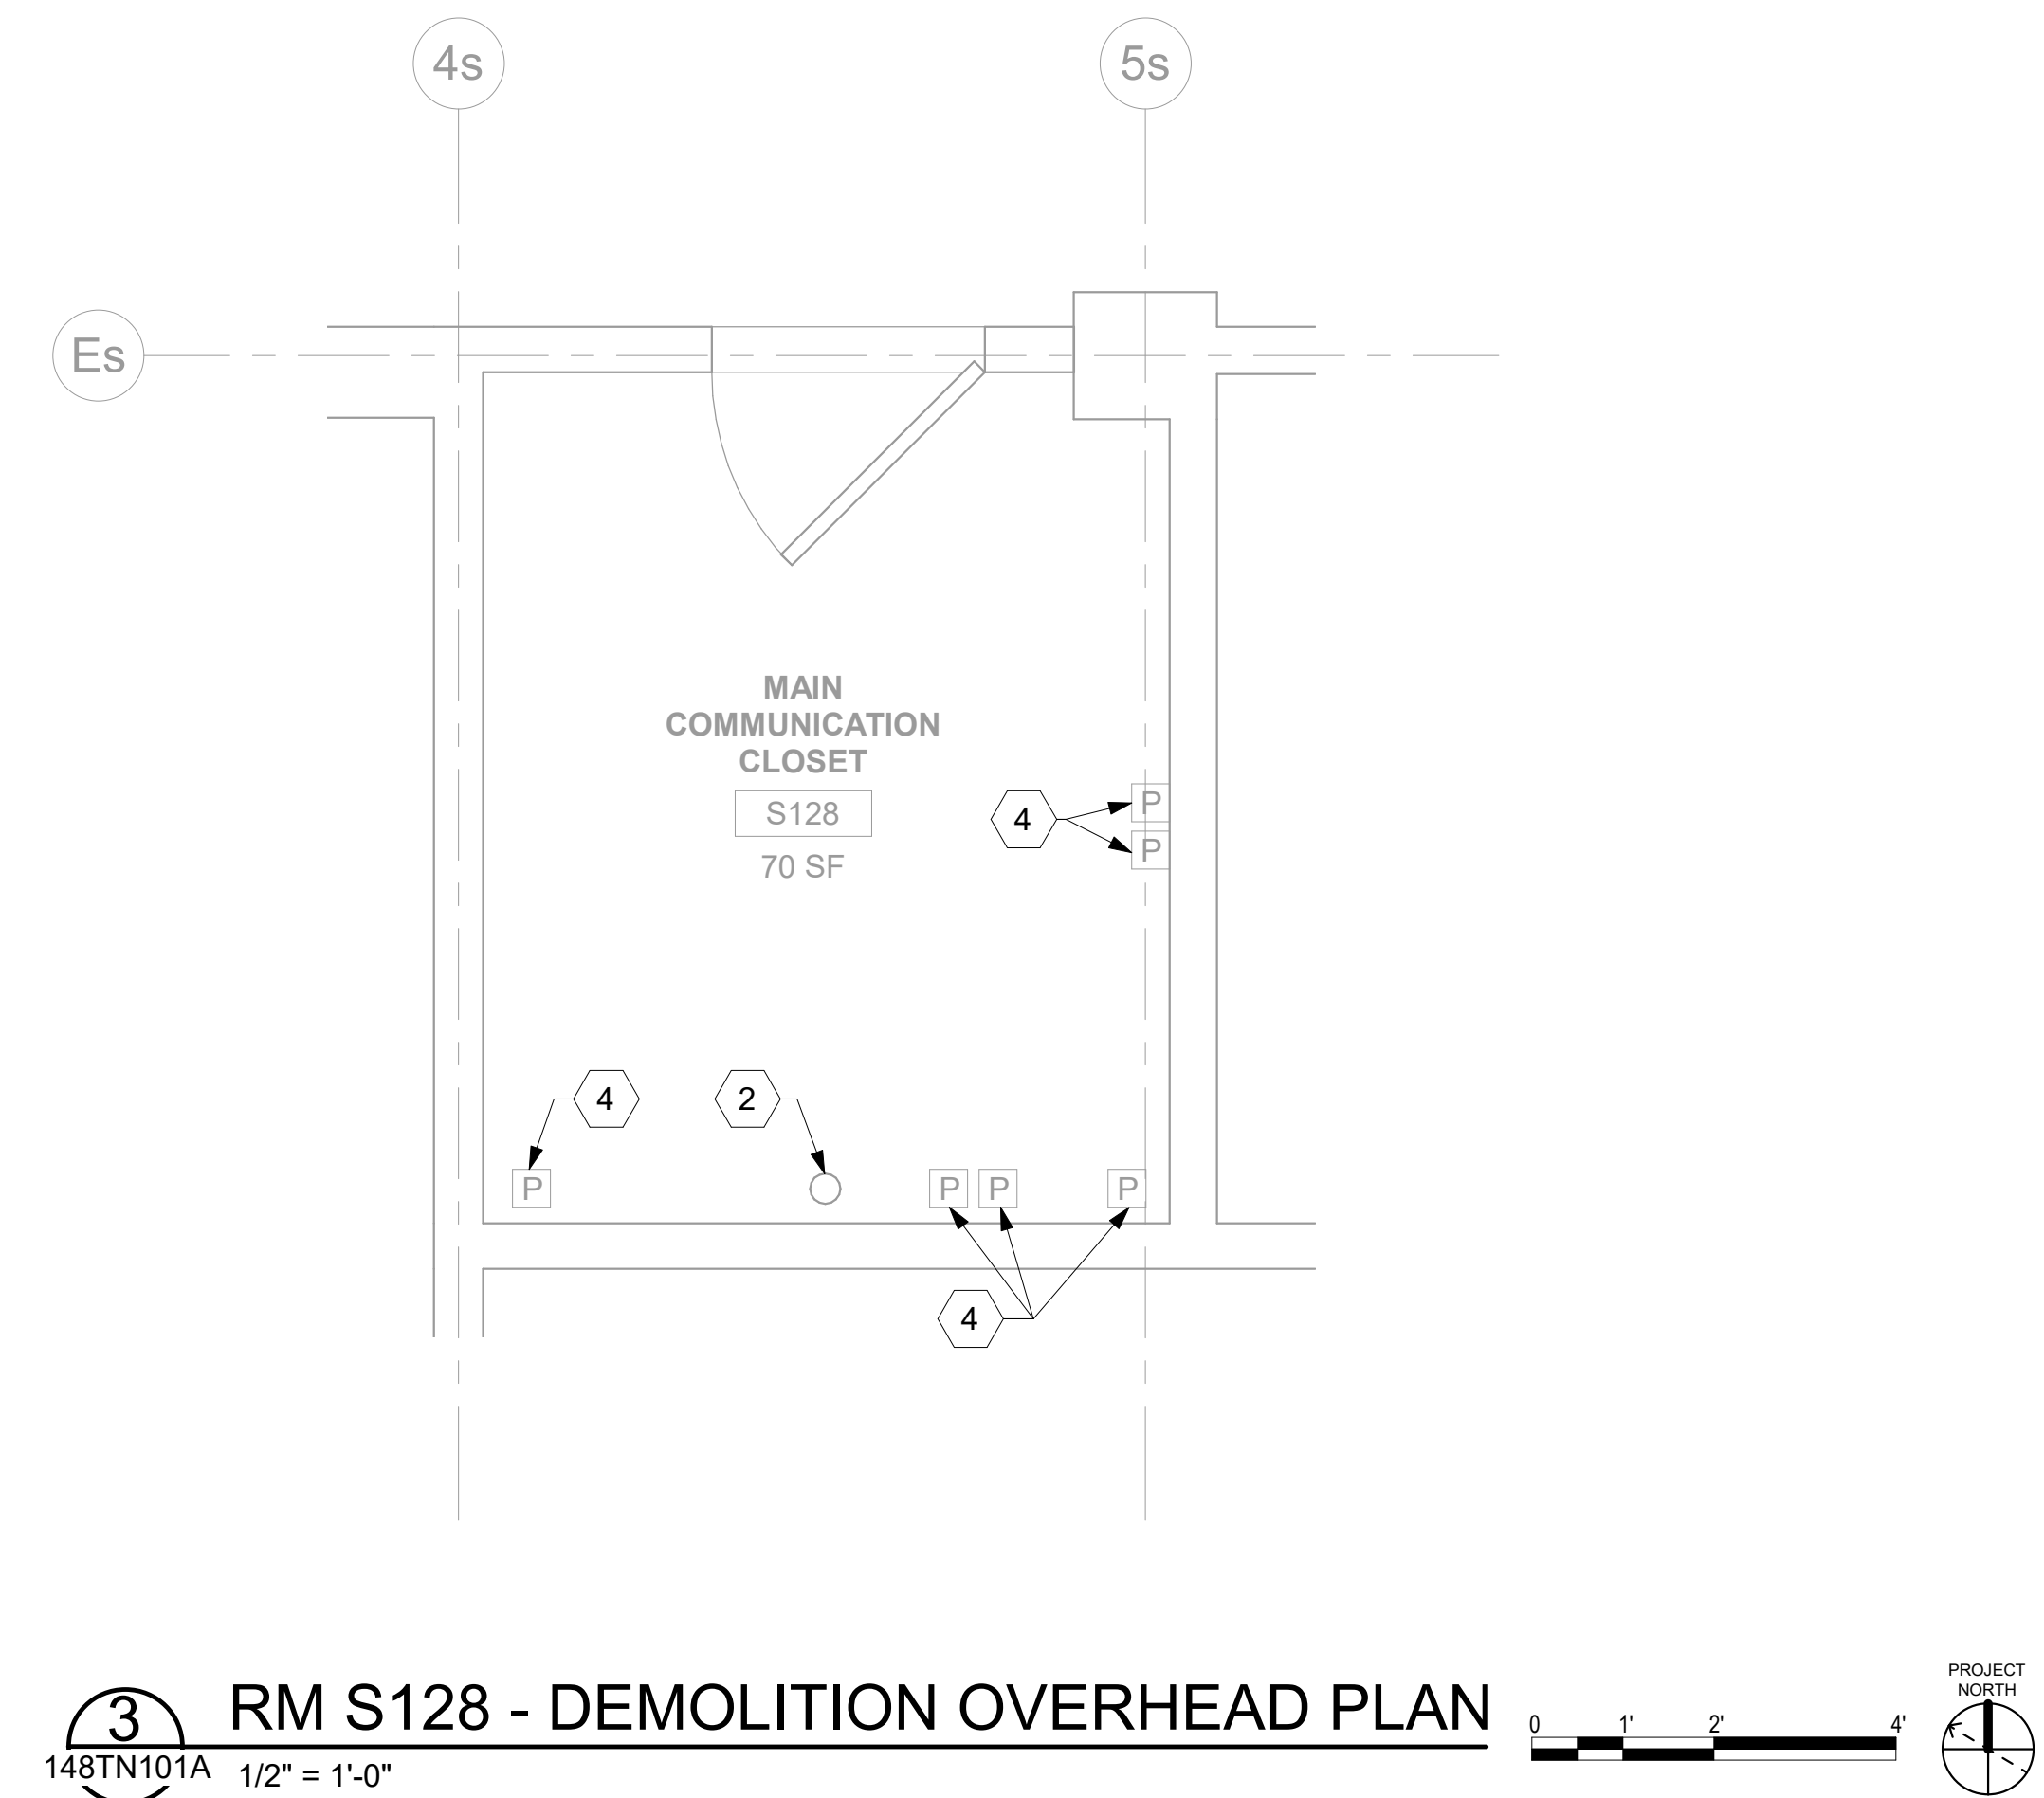

3 RM S128 - DEMOLITION OVERHEAD PLAN

148TN101A 1/2" = 1'-0"

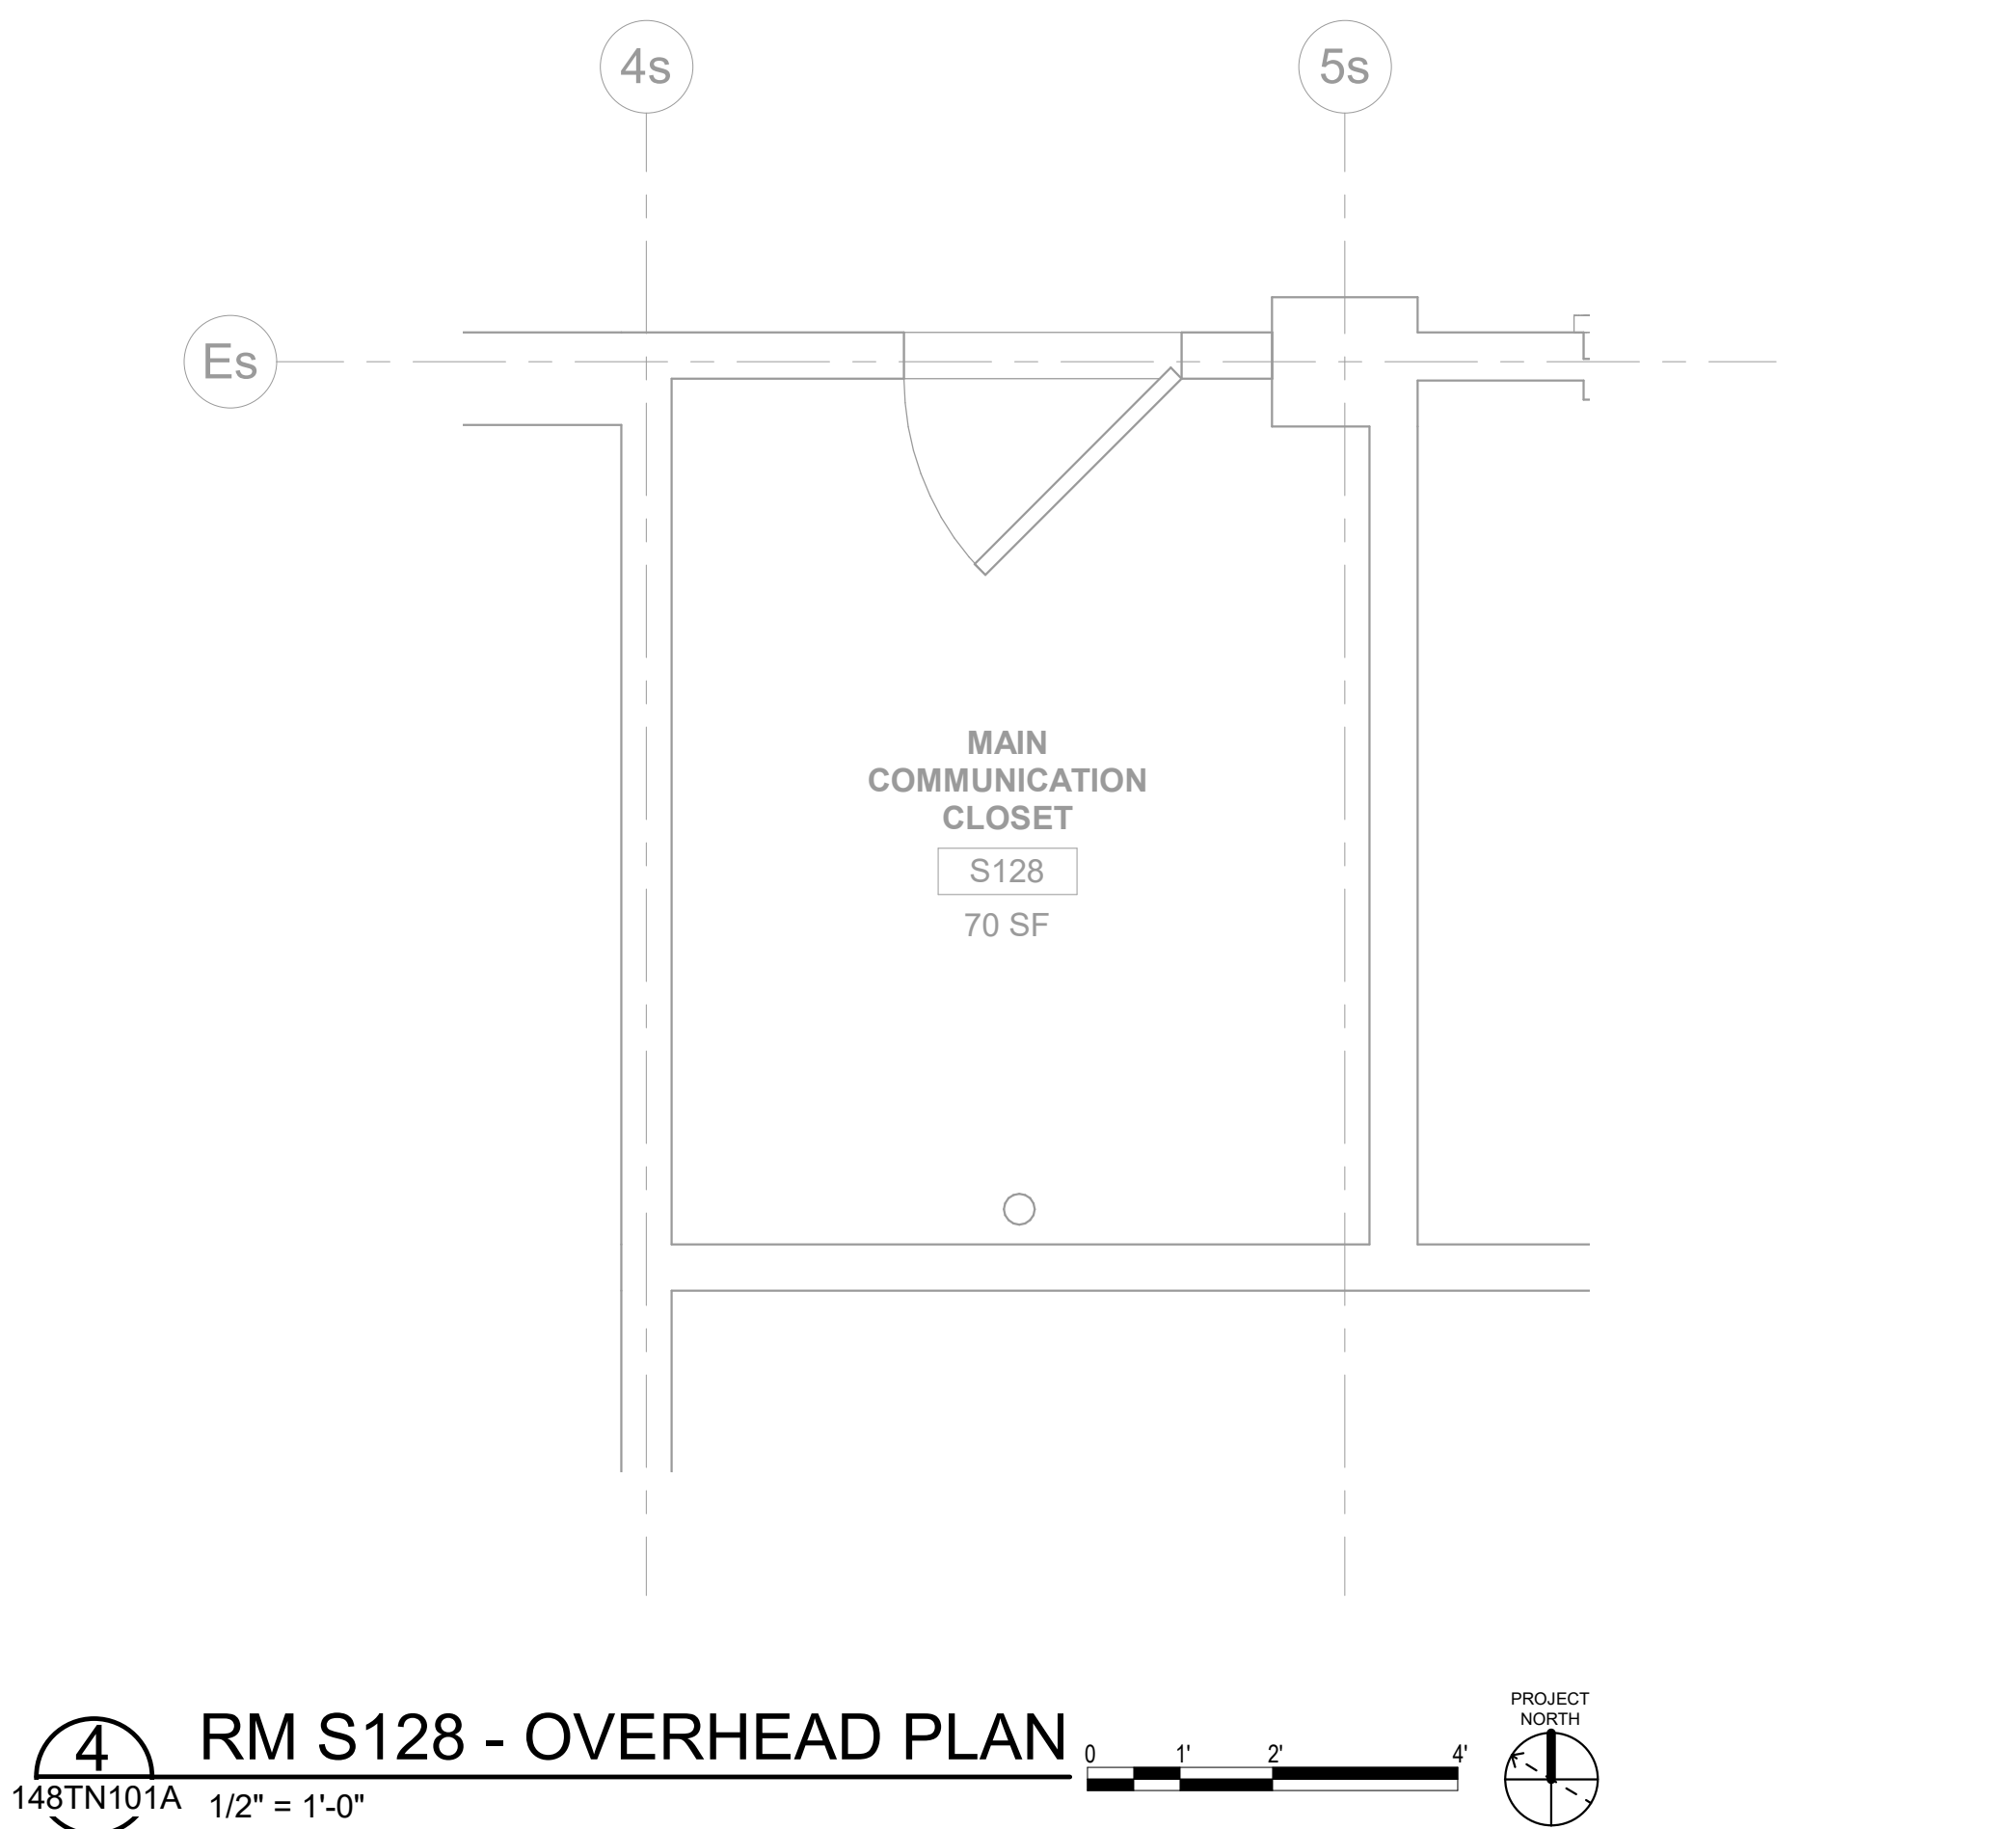

4 RM S128 - OVERHEAD PLAN

148TN101A 1/2" = 1'-0"

BM 360/599-22-700
Washington EHRMEE - BLDG
148-11
15/07/2025 11:11:47 am

VA FORM 08 - 6231

CONSULTANT

ENGINEERING DISCIPLINE:

ARCHITECT/ENGINEER OF RECORD

A/E:
SPEES DESIGN BUILD
23830 PACIFIC HIGHWAY S. SUITE 203
KENT, WA 98032



STAMP



Office of
Construction
and Facilities
Management



U.S. Department
of Veterans Affairs

Drawing Title

BLDG 148 - LEVEL 01 - ENLARGED
TELECOMMUNICATIONS PLANS

Approved:

Phase

100% CONSTRUCTION
DOCUMENTS

FULLY SPRINKLERED

Project Title

EHRM INFRASTRUCTURE
UPGRADES - HAMPTON

Issue Date

07/18/2025

Checked

KG

Drawn

BCL/GPB

Project Number

590-22-700

Building Number

148

Drawing Number

148TN401j

614 of 713


GENERAL NOTES

- PROTECT ALL EXISTING WORK FROM DAMAGE DURING CONSTRUCTION. ANY DAMAGED MATERIALS, SYSTEMS, COMPONENTS, FINISHES AND THE LIKE, SHALL BE REPAIRED OR REPLACED AT THE EXPENSE OF THE CONTRACTOR TO THE ACCEPTANCE OF THE OWNER.
- SEAL ALL INTERIOR WALL AND CEILING PENETRATIONS TO MATCH EXISTING FIRE RATING OR NEW FIRE RATING, IF REQUIRED. COORDINATE WITH ARCHITECTURAL DRAWINGS AS REQUIRED.
- ALL TELECOMMUNICATIONS CABLING CATEGORY 6 AND BELOW SHALL BE REMOVED AND REPLACED WITH CAT6A PORTS AND CABLE QUANTITIES INDICATED, UNLESS NOTED OTHERWISE.
- TELECOMMUNICATIONS CABLES SHALL BE ROUTED IN EXISTING PATHWAY VACATED BY EXISTING CABLING. PROVIDE RACEWAYS TO EXTEND TO ASSOCIATED TR.
- A TELECOMMUNICATIONS OUTLET UPGRADE SHALL INCLUDE, BUT IS NOT LIMITED TO REMOVING AND DISPOSING EXISTING DEVICES AND CABLES; PROVIDING ALL LABOR, MATERIALS, TOOLS, TEST INSTRUMENTS, AND CONSUMABLES REQUIRED FOR THE INSTALLATION, TERMINATION, TESTING, LABELING, AND CERTIFICATION OF A FULLY FUNCTIONAL CATEGORY 6A OUTLET WITH THE PORT QUANTITY INDICATED.
- WHERE NEW DATA OUTLETS ARE BEING PROVIDED AND EXISTING DATA OUTLET CURRENTLY DOES NOT EXIST, PROVIDE (1) 1" CONDUIT FROM NEW BACKBOX TO ACCESSIBLE CEILING SPACE TO SECURELY ROUTE DATA CABLING FROM OUTLET TO TR VIA CABLE TRAY. IF CABLE TRAY IS NON-EXISTENT, EXTEND RACEWAY FROM OUTLET TO TR AS REQUIRED.
- PROVIDE CONDUITS AND SLEEVES AS REQUIRED FOR ROUTING AND INSTALLATION OF HORIZONTAL AND BACKBONE CABLING. PROVIDE FIRE-STOP MATERIALS TO SEAL IN AND AROUND CONDUIT PER CODE. REFER TO ARCHITECTURAL DRAWINGS FOR PARTITION TYPES AND WALL HEIGHTS.
- ALL TELECOMMUNICATION ROOMS SHALL BE PROVIDED WITH FIRE-RATED PLYWOOD BACKBOARDS. REFERENCE EXACT PLACEMENTS WITH ARCHITECTURE DRAWINGS AS REQUIRED.
- ANY LIVE SYSTEMS IN DEMO'D TR'S MUST REMAIN LIVE. CONTRACTOR TO COORDINATE WITH THE STATION TO IDENTIFY SYSTEMS THAT ARE LIVE. IF SYSTEMS ARE LIVE; INSTALL NEW CABLE FROM DEMO'D TR TO NEW TR. REFER TO DETAIL '3' ON TN506.

KEY NOTES

- EXISTING DATA RACK TO BE DECOMMISSIONED BY VA. CONTRACTOR SHALL COORDINATE WITH VA AS REQUIRED.
- EXISTING VERTICAL CABLING SLEEVE TO BE PRESERVED. EXISTING FIBER OPTIC AND/OR EXISTING VERTICAL CABLING RELATED TO EXISTING TR RACKS TO BE DEMOLISHED.

KEY PLAN

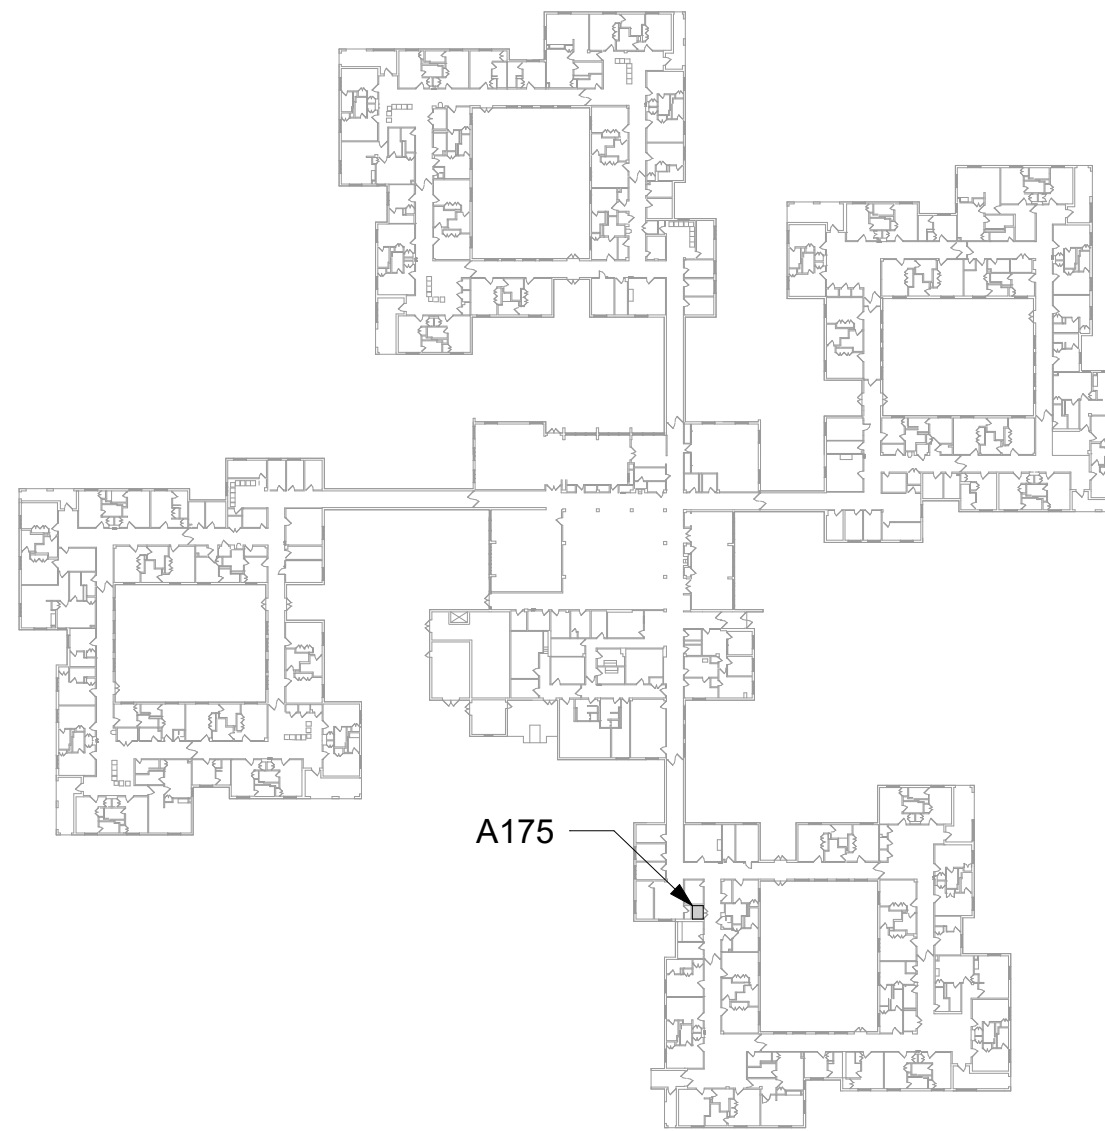


AREA SHOWN




1 RM A175 - DEMOLITION FLOOR PLAN

148TN101A 1/2" = 1'-0"

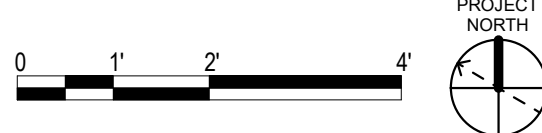


2 RM A175 - TELECOMMUNICATIONS PLAN

148TN101A 1/2" = 1'-0"

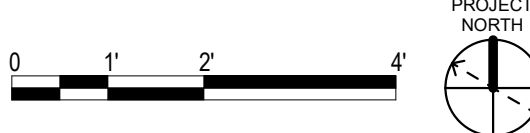


3 RM A175 - DEMOLITION OVERHEAD PLAN

148TN101A 1/2" = 1'-0"

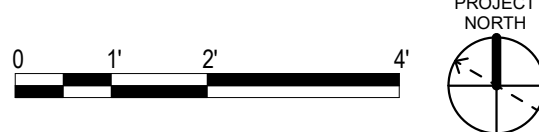

4 RM A175 - OVERHEAD PLAN

148TN101A 1/2" = 1'-0"

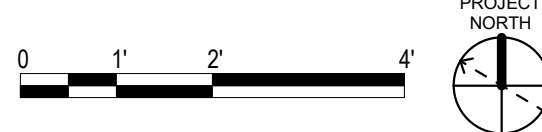



GENERAL NOTES

1. PROTECT ALL EXISTING WORK FROM DAMAGE DURING CONSTRUCTION. ANY DAMAGED MATERIALS, SYSTEMS, COMPONENTS, FINISHES AND THE LIKE, SHALL BE REPAIRED OR REPLACED AT THE EXPENSE OF THE CONTRACTOR TO THE ACCEPTANCE OF THE OWNER.
2. SEAL ALL INTERIOR WALL AND CEILING PENETRATIONS TO MATCH EXISTING FIRE RATING OR NEW FIRE RATING, IF REQUIRED. COORDINATE WITH ARCHITECTURAL DRAWINGS AS REQUIRED.
3. ALL TELECOMMUNICATIONS CABLING CATEGORY 6 AND BELOW SHALL BE REMOVED AND REPLACED WITH CAT6A PORTS AND CABLE QUANTITIES INDICATED, UNLESS NOTED OTHERWISE.
4. TELECOMMUNICATIONS CABLES SHALL BE ROUTED IN EXISTING PATHWAY VACATED BY EXISTING CABLING. PROVIDE RACEWAYS TO EXTEND TO ASSOCIATED TR.
5. A TELECOMMUNICATIONS OUTLET UPGRADE SHALL INCLUDE, BUT IS NOT LIMITED TO REMOVING AND DISPOSING EXISTING DEVICES AND CABLES; PROVIDING ALL LABOR, MATERIALS, TOOLS, TEST INSTRUMENTS, AND CONSUMABLES REQUIRED FOR THE INSTALLATION, TERMINATION, TESTING, LABELING, AND CERTIFICATION OF A FULLY FUNCTIONAL CATEGORY 6A OUTLET WITH THE PORT QUANTITY INDICATED.
6. WHERE NEW DATA OUTLETS ARE BEING PROVIDED AND EXISTING DATA OUTLET CURRENTLY DOES NOT EXIST, PROVIDE (1) 1" CONDUIT FROM NEW BACKBOX TO ACCESSIBLE CEILING SPACE TO SECURELY ROUTE DATA CABLING FROM OUTLET TO TR VIA CABLE TRAY. IF CABLE TRAY IS NON-EXISTENT, EXTEND RACEWAY FROM OUTLET TO TR AS REQUIRED.
7. PROVIDE CONDUITS AND SLEEVES AS REQUIRED FOR ROUTING AND INSTALLATION OF HORIZONTAL AND BACKBONE CABLING. PROVIDE FIRE-STOP MATERIALS TO SEAL IN AND AROUND CONDUIT PER CODE. REFER TO ARCHITECTURAL DRAWINGS FOR PARTITION TYPES AND WALL HEIGHTS.
8. ALL TELECOMMUNICATION ROOMS SHALL BE PROVIDED WITH FIRE-RATED PLYWOOD BACKBOARDS. REFERENCE EXACT PLACEMENTS WITH ARCHITECTURE DRAWINGS AS REQUIRED.
9. ANY LIVE SYSTEMS IN DEMO'D TR'S MUST REMAIN LIVE. CONTRACTOR TO COORDINATE WITH THE STATION TO IDENTIFY SYSTEMS THAT ARE LIVE. IF SYSTEMS ARE LIVE, INSTALL NEW CABLE FROM DEMO'D TR TO NEW TR. REFER TO DETAIL '3' ON TN506.
10. RAIL KITS ARE PROVIDED BY THE GC FOR EQUIPMENT MOUNTED IN THE TR CHANNEL RACKS.
11. LADDER RACK IN ALL TR'S WILL BE MOUNTED 6" OFF THE WALLS TO ACCOMMODATE ELECTRICAL AND MECHNICAL EQUIPMENT.

KEY NOTES


- 1 EXISTING DATA RACK TO BE DECOMMISSIONED BY VA. CONTRACTOR SHALL COORDINATE WITH VA AS REQUIRED.
- 2 EXISTING EQUIPMENT TO BE DEMOLISHED. ASSOCIATED RACEWAYS AND CABLING SHALL BE DEMOLISHED BACK TO SOURCE.
- 3 PROVIDE RIGID CONDUIT SLEEVES WITH FIRE PROOFING AS REQUIRED. SIDE 'A' AND SIDE 'B' SLEEVES SHALL BE SEPARATED BY AT LEAST 10-FT.
- 4 WIRE BASKET CABLE TRAY.
- 5 EXISTING VERTICAL CABLING SLEEVES (QTY = 7) TO BE DEMOLISHED. EXISTING CABLING TO BE DEMOLISHED AND REMOVED.
- 6 EXISTING VERTICAL CABLING SLEEVE TO BE PRESERVED. EXISTING FIBER OPTIC AND/OR EXISTING VERTICAL CABLING RELATED TO EXISTING TR RACKS TO BE DEMOLISHED.
- 7 EXISTING PENETRATIONS WITH CABLING TO BE REMOVED. CONTRACTOR SHALL PATCH AND FIREPROOF OPENINGS. COORDINATE WITH ARCHITECTURAL DRAWINGS AND SPECIFICATIONS.
- 8 EXISTING EQUIPMENT TO BE RELOCATED AS SHOWN IN DETAIL '2' ON THIS SHEET.
- 9 RELOCATED EQUIPMENT. PROVIDE TEMPORARY PANELS OR EQUIPMENT AS REQUIRED TO ENSURE FULLY FUNCTIONAL ACCESS CONTROL AND FIRE ALARM SYSTEMS DURING RELOCATION. EXTEND CONDUIT AND WIRE TO RELOCATED EQUIPMENT AS REQUIRED.
- 10 PROVIDE (2)-DOOR ACCESS CONTROL PANEL TO SERVE ALL PACS DOOR SECURITY EQUIPMENT FOR THIS TR ROOM. PROVIDE ALL REQUIRED CONNECTIONS, PROGRAMMING, POWER SUPPLIES, AND COMPONENTS TO PROVIDE A COMPLETE AND FULLY FUNCTIONAL SYSTEM. REFERENCE SPECIFICATION "28 13 00 - PHYSICAL ACCESS CONTROL SYSTEM" FOR ADDITIONAL INFORMATION.

KEY PLAN

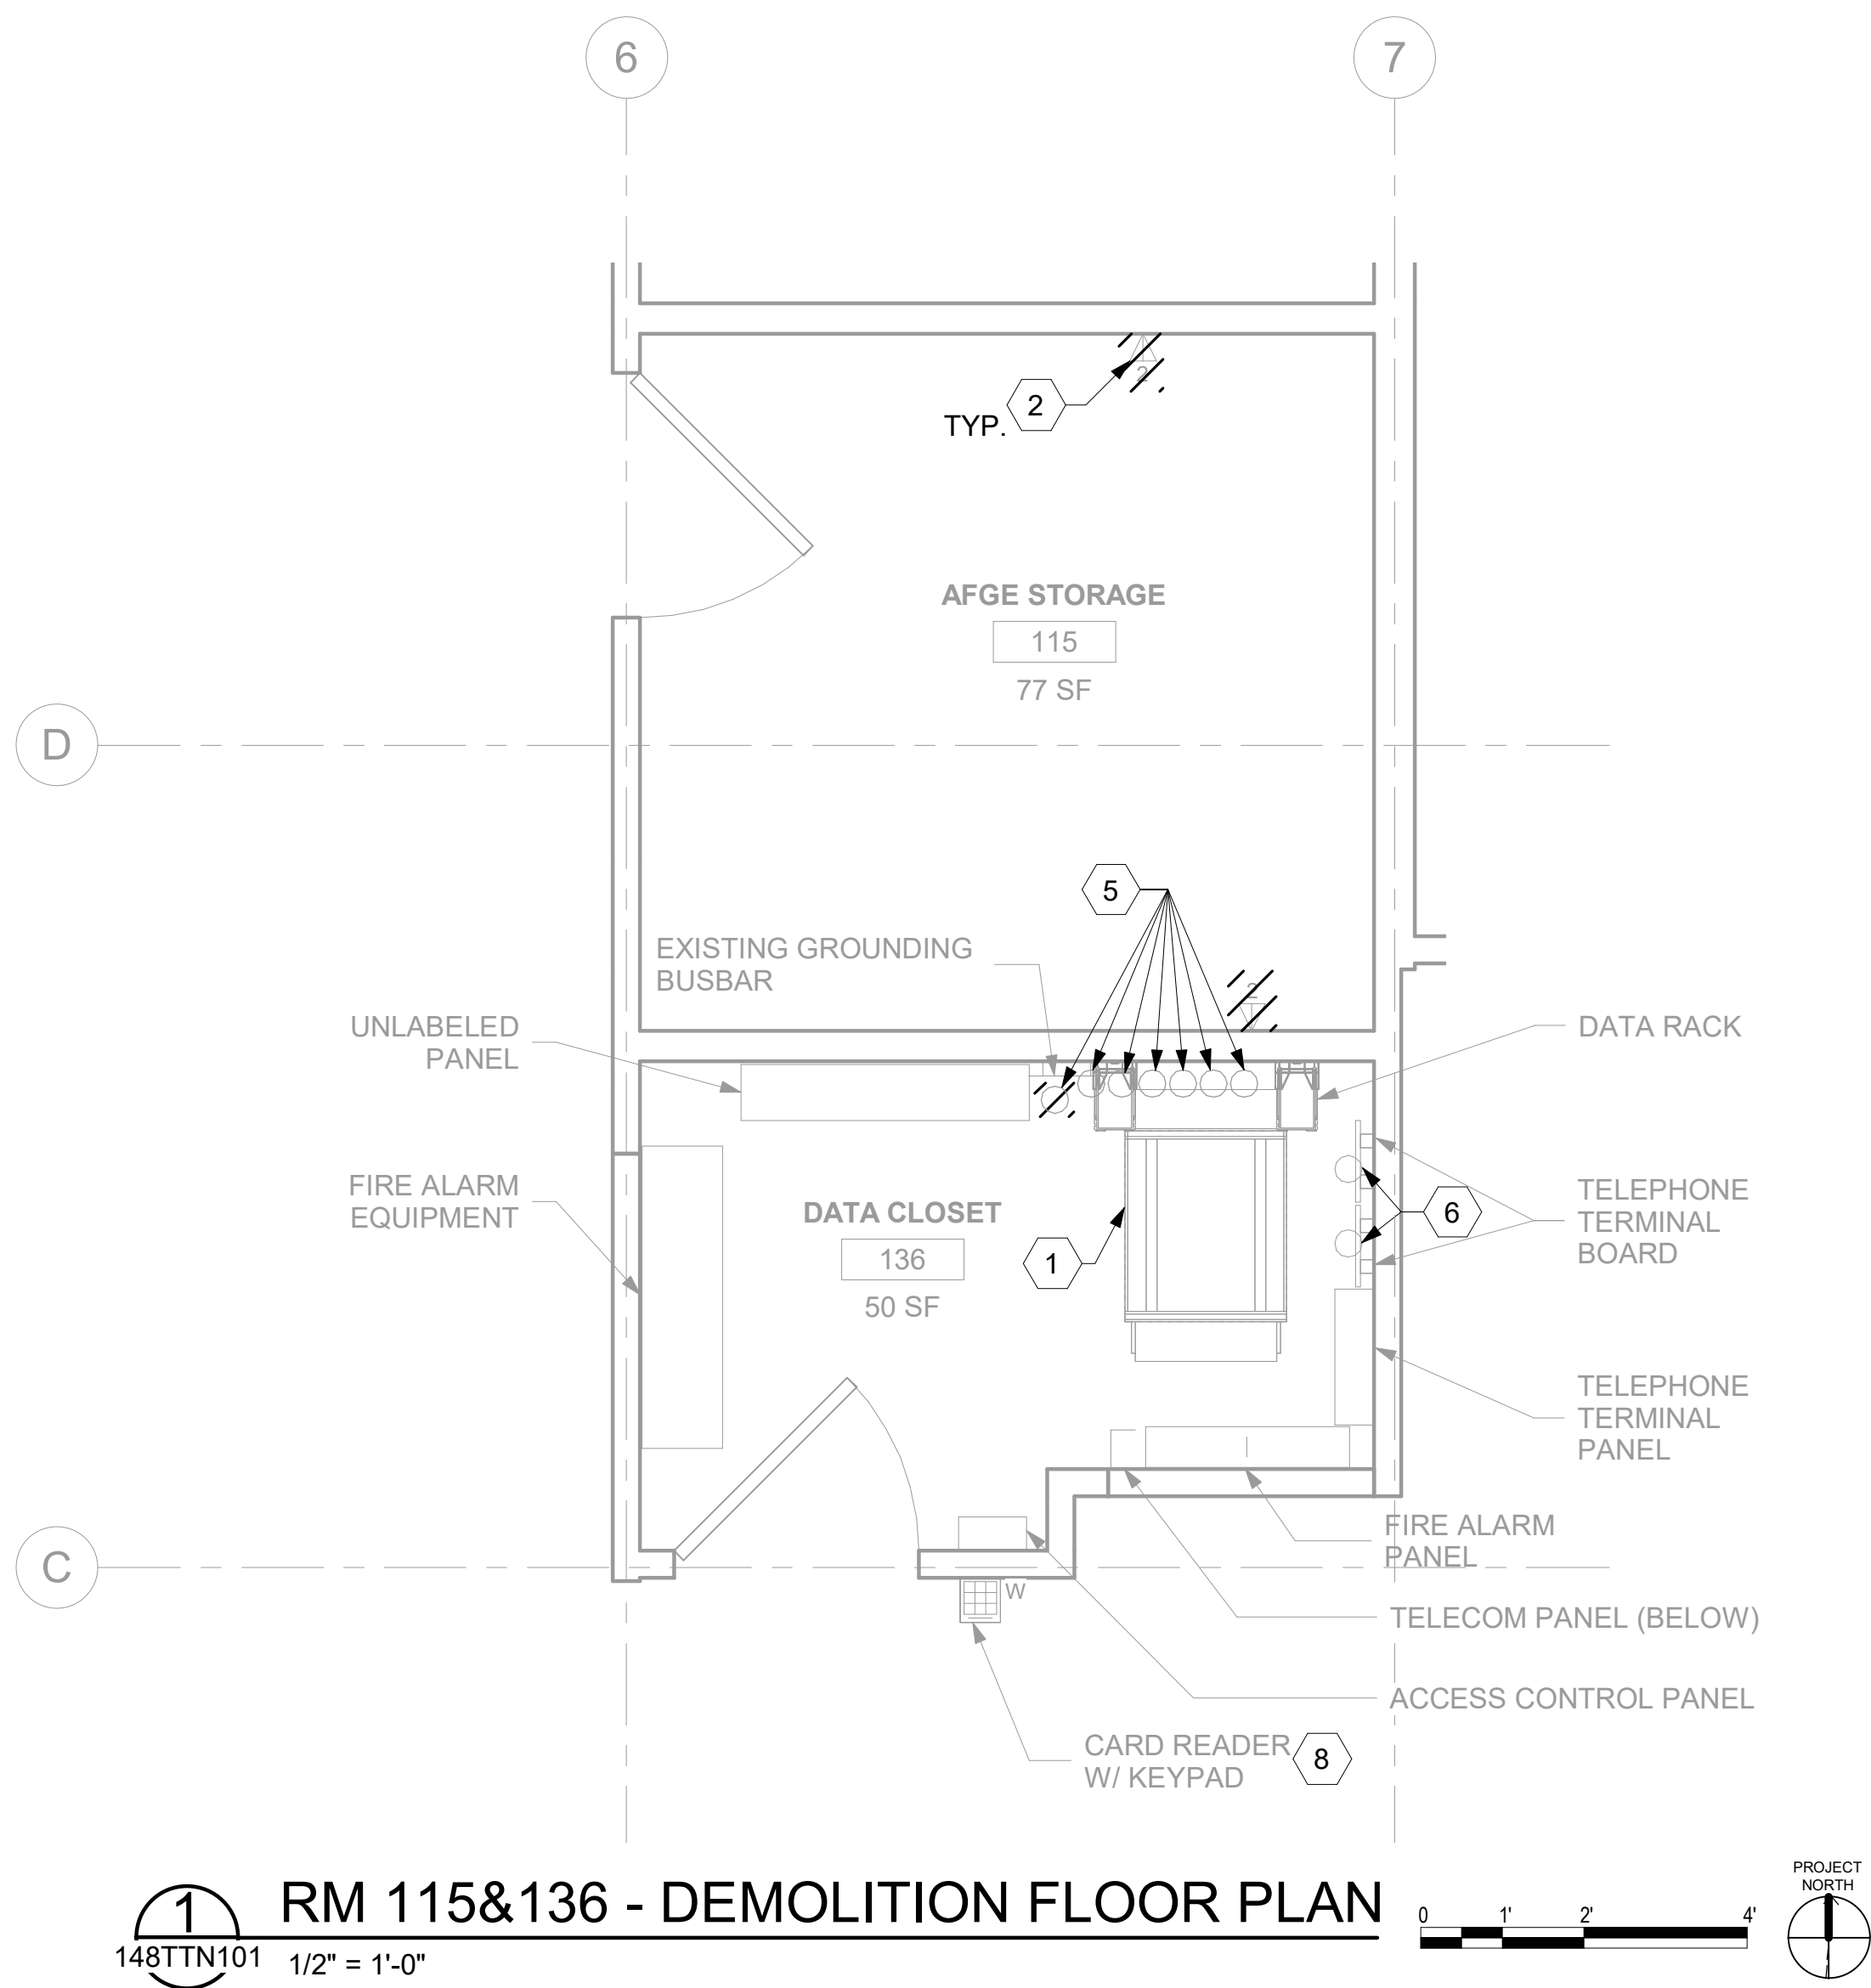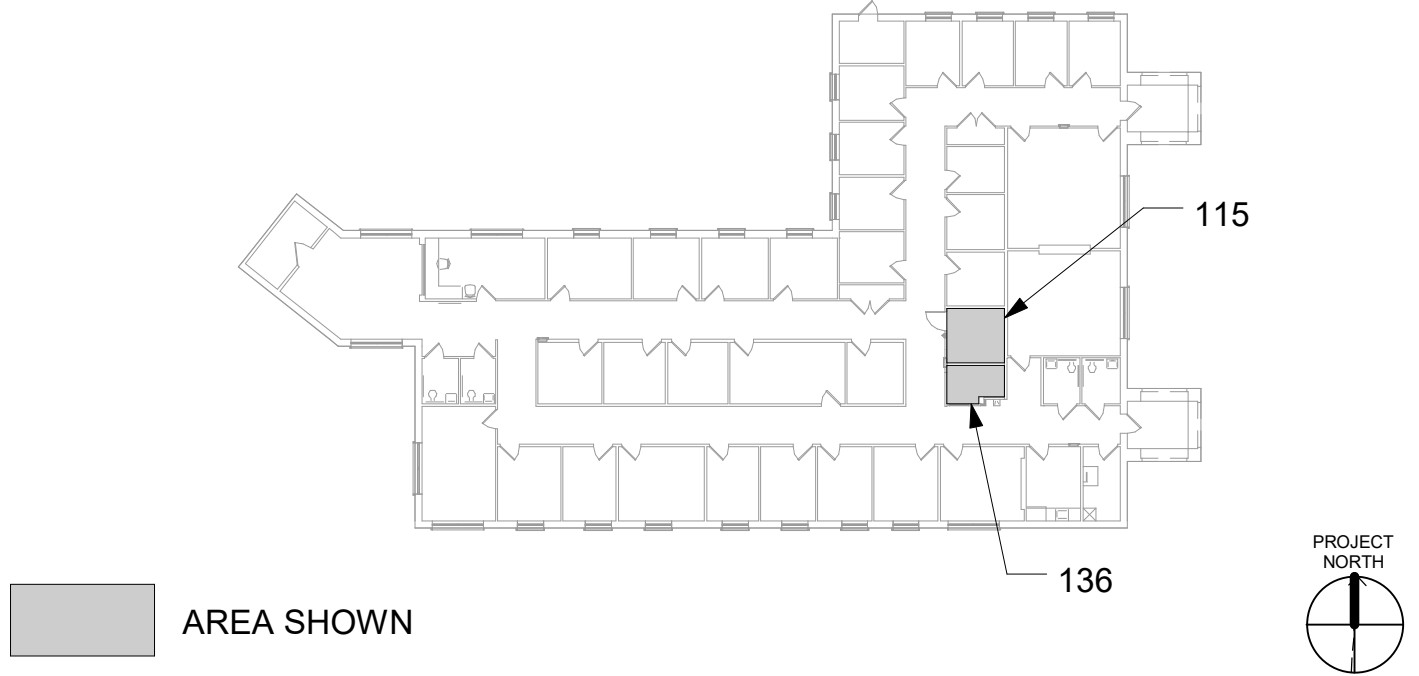


1 RM 115&136 - DEMOLITION FLOOR PLAN

148TTN101 1/2" = 1'-0"

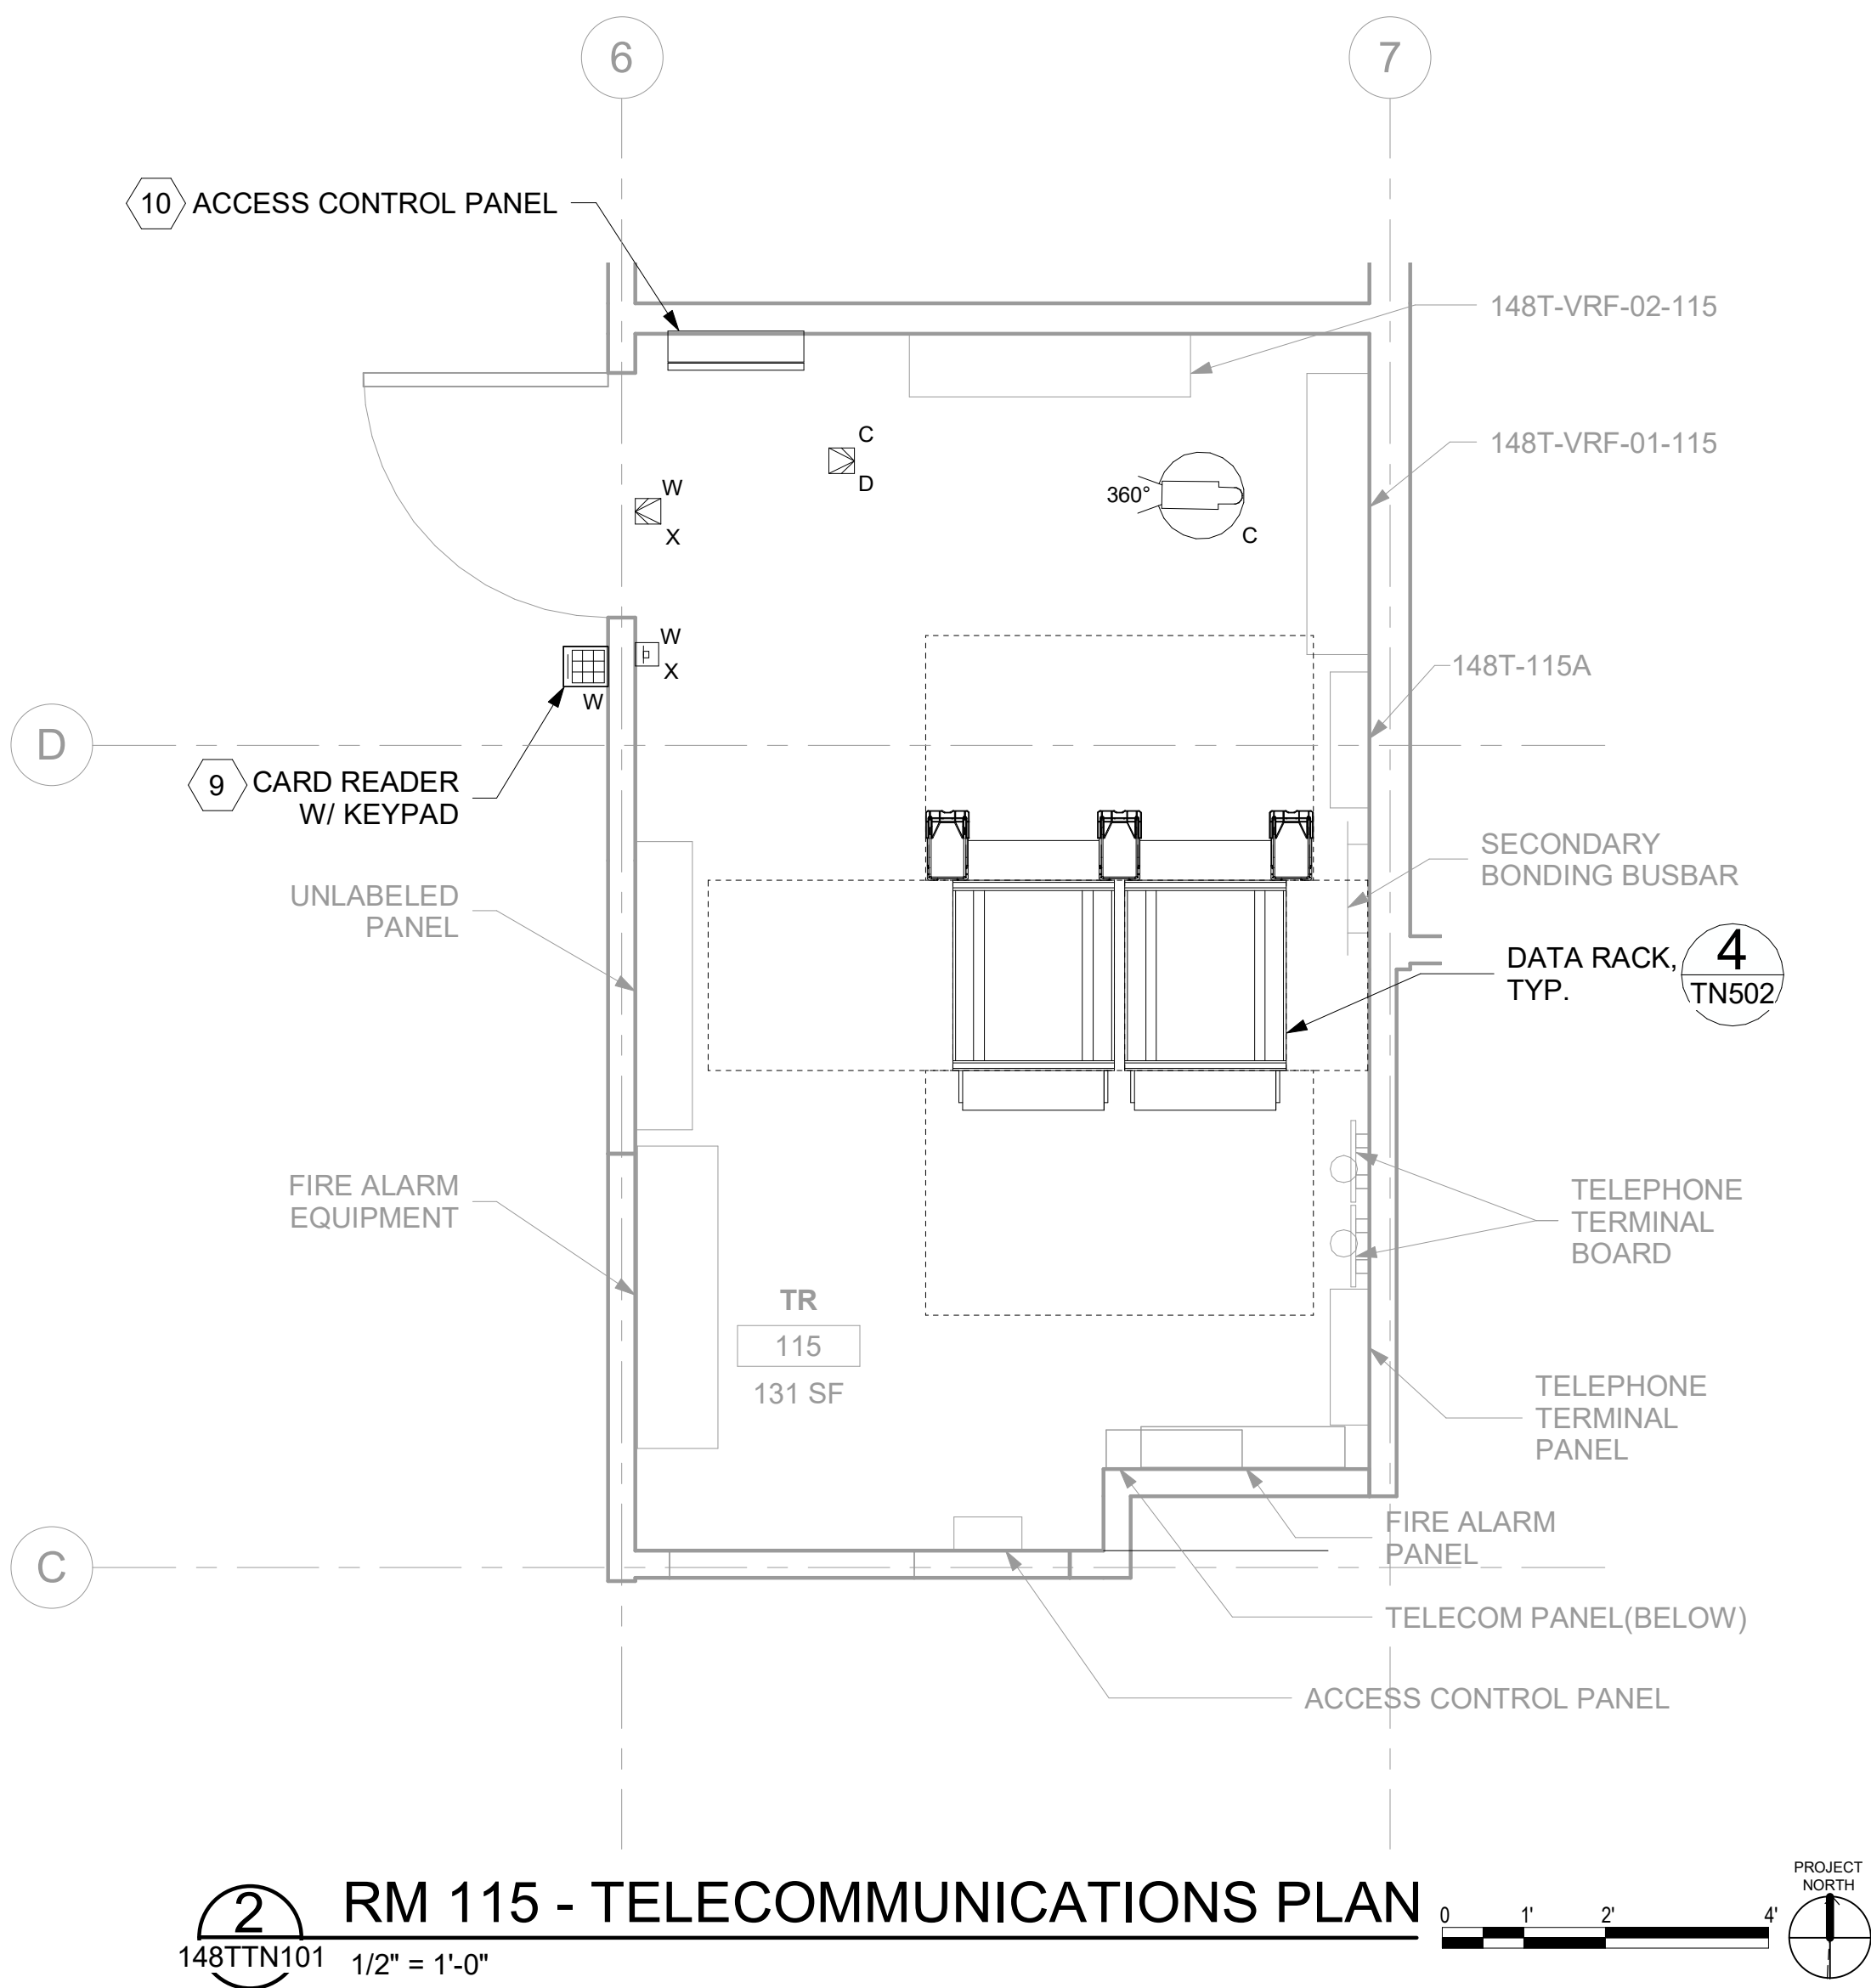


2 RM 115 - TELECOMMUNICATIONS PLAN

148TTN101 1/2" = 1'-0"

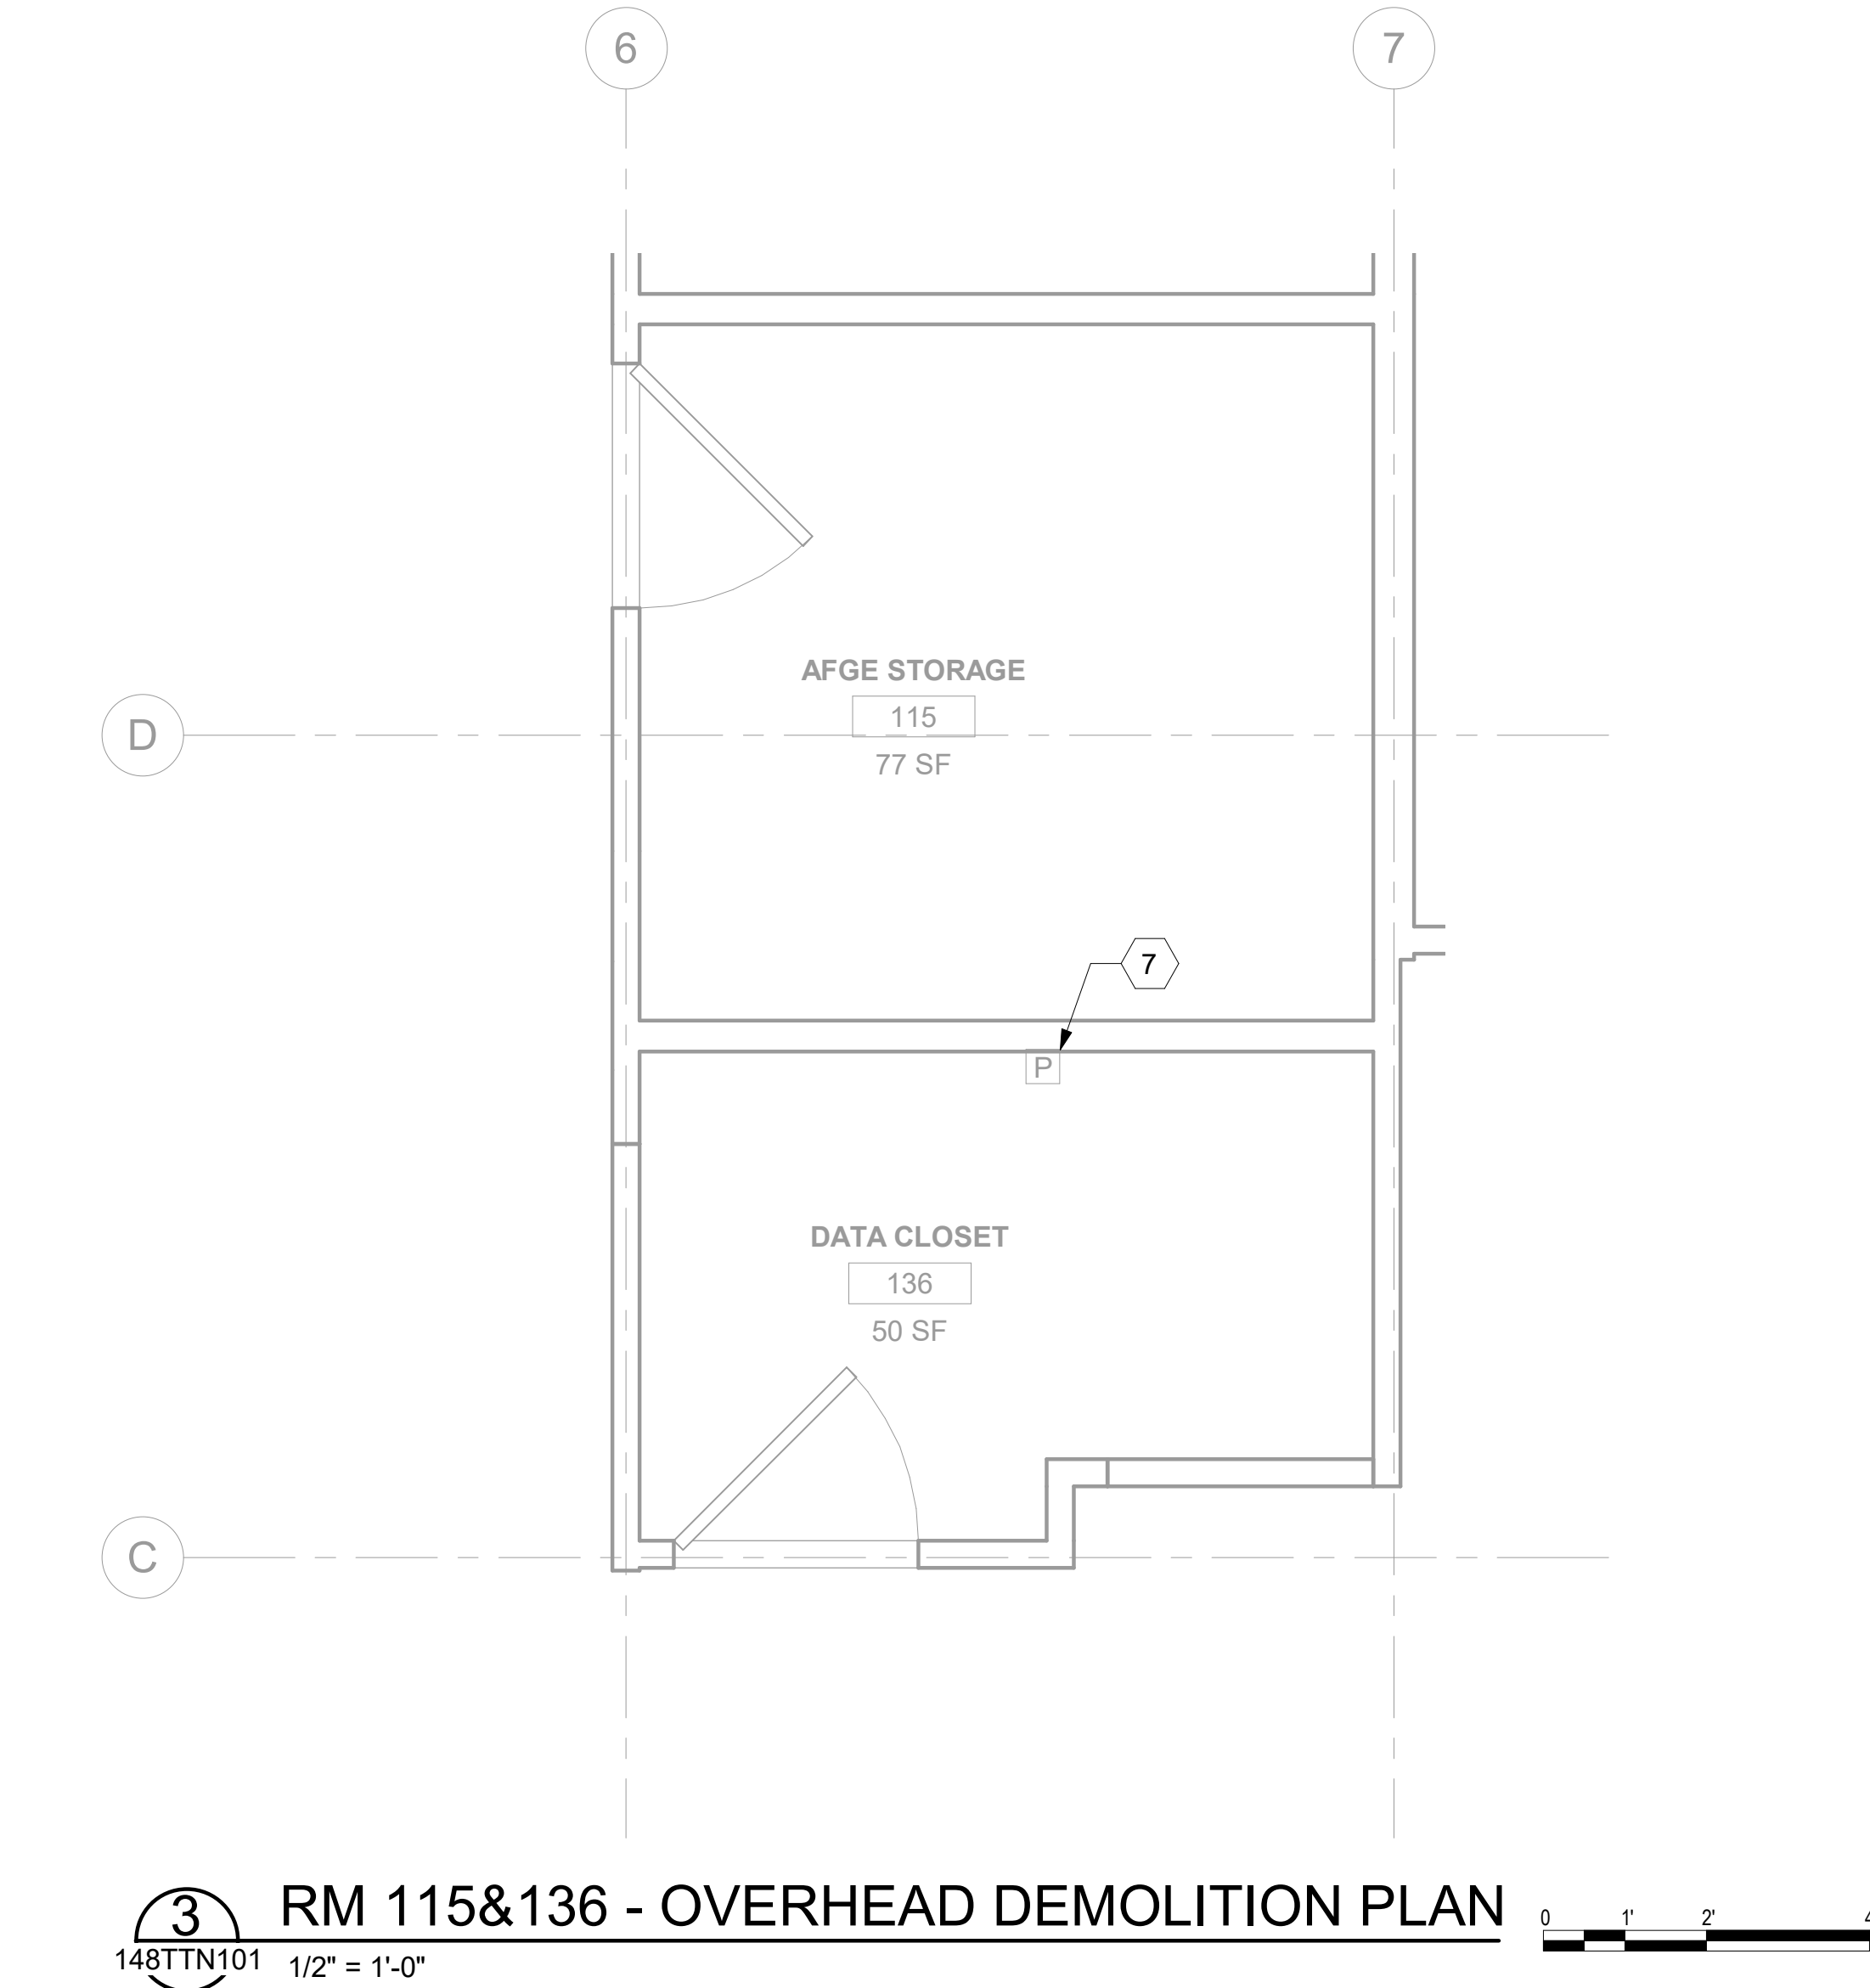

3 RM 115&136 - OVERHEAD DEMOLITION PLAN

148TTN101 1/2" = 1'-0"

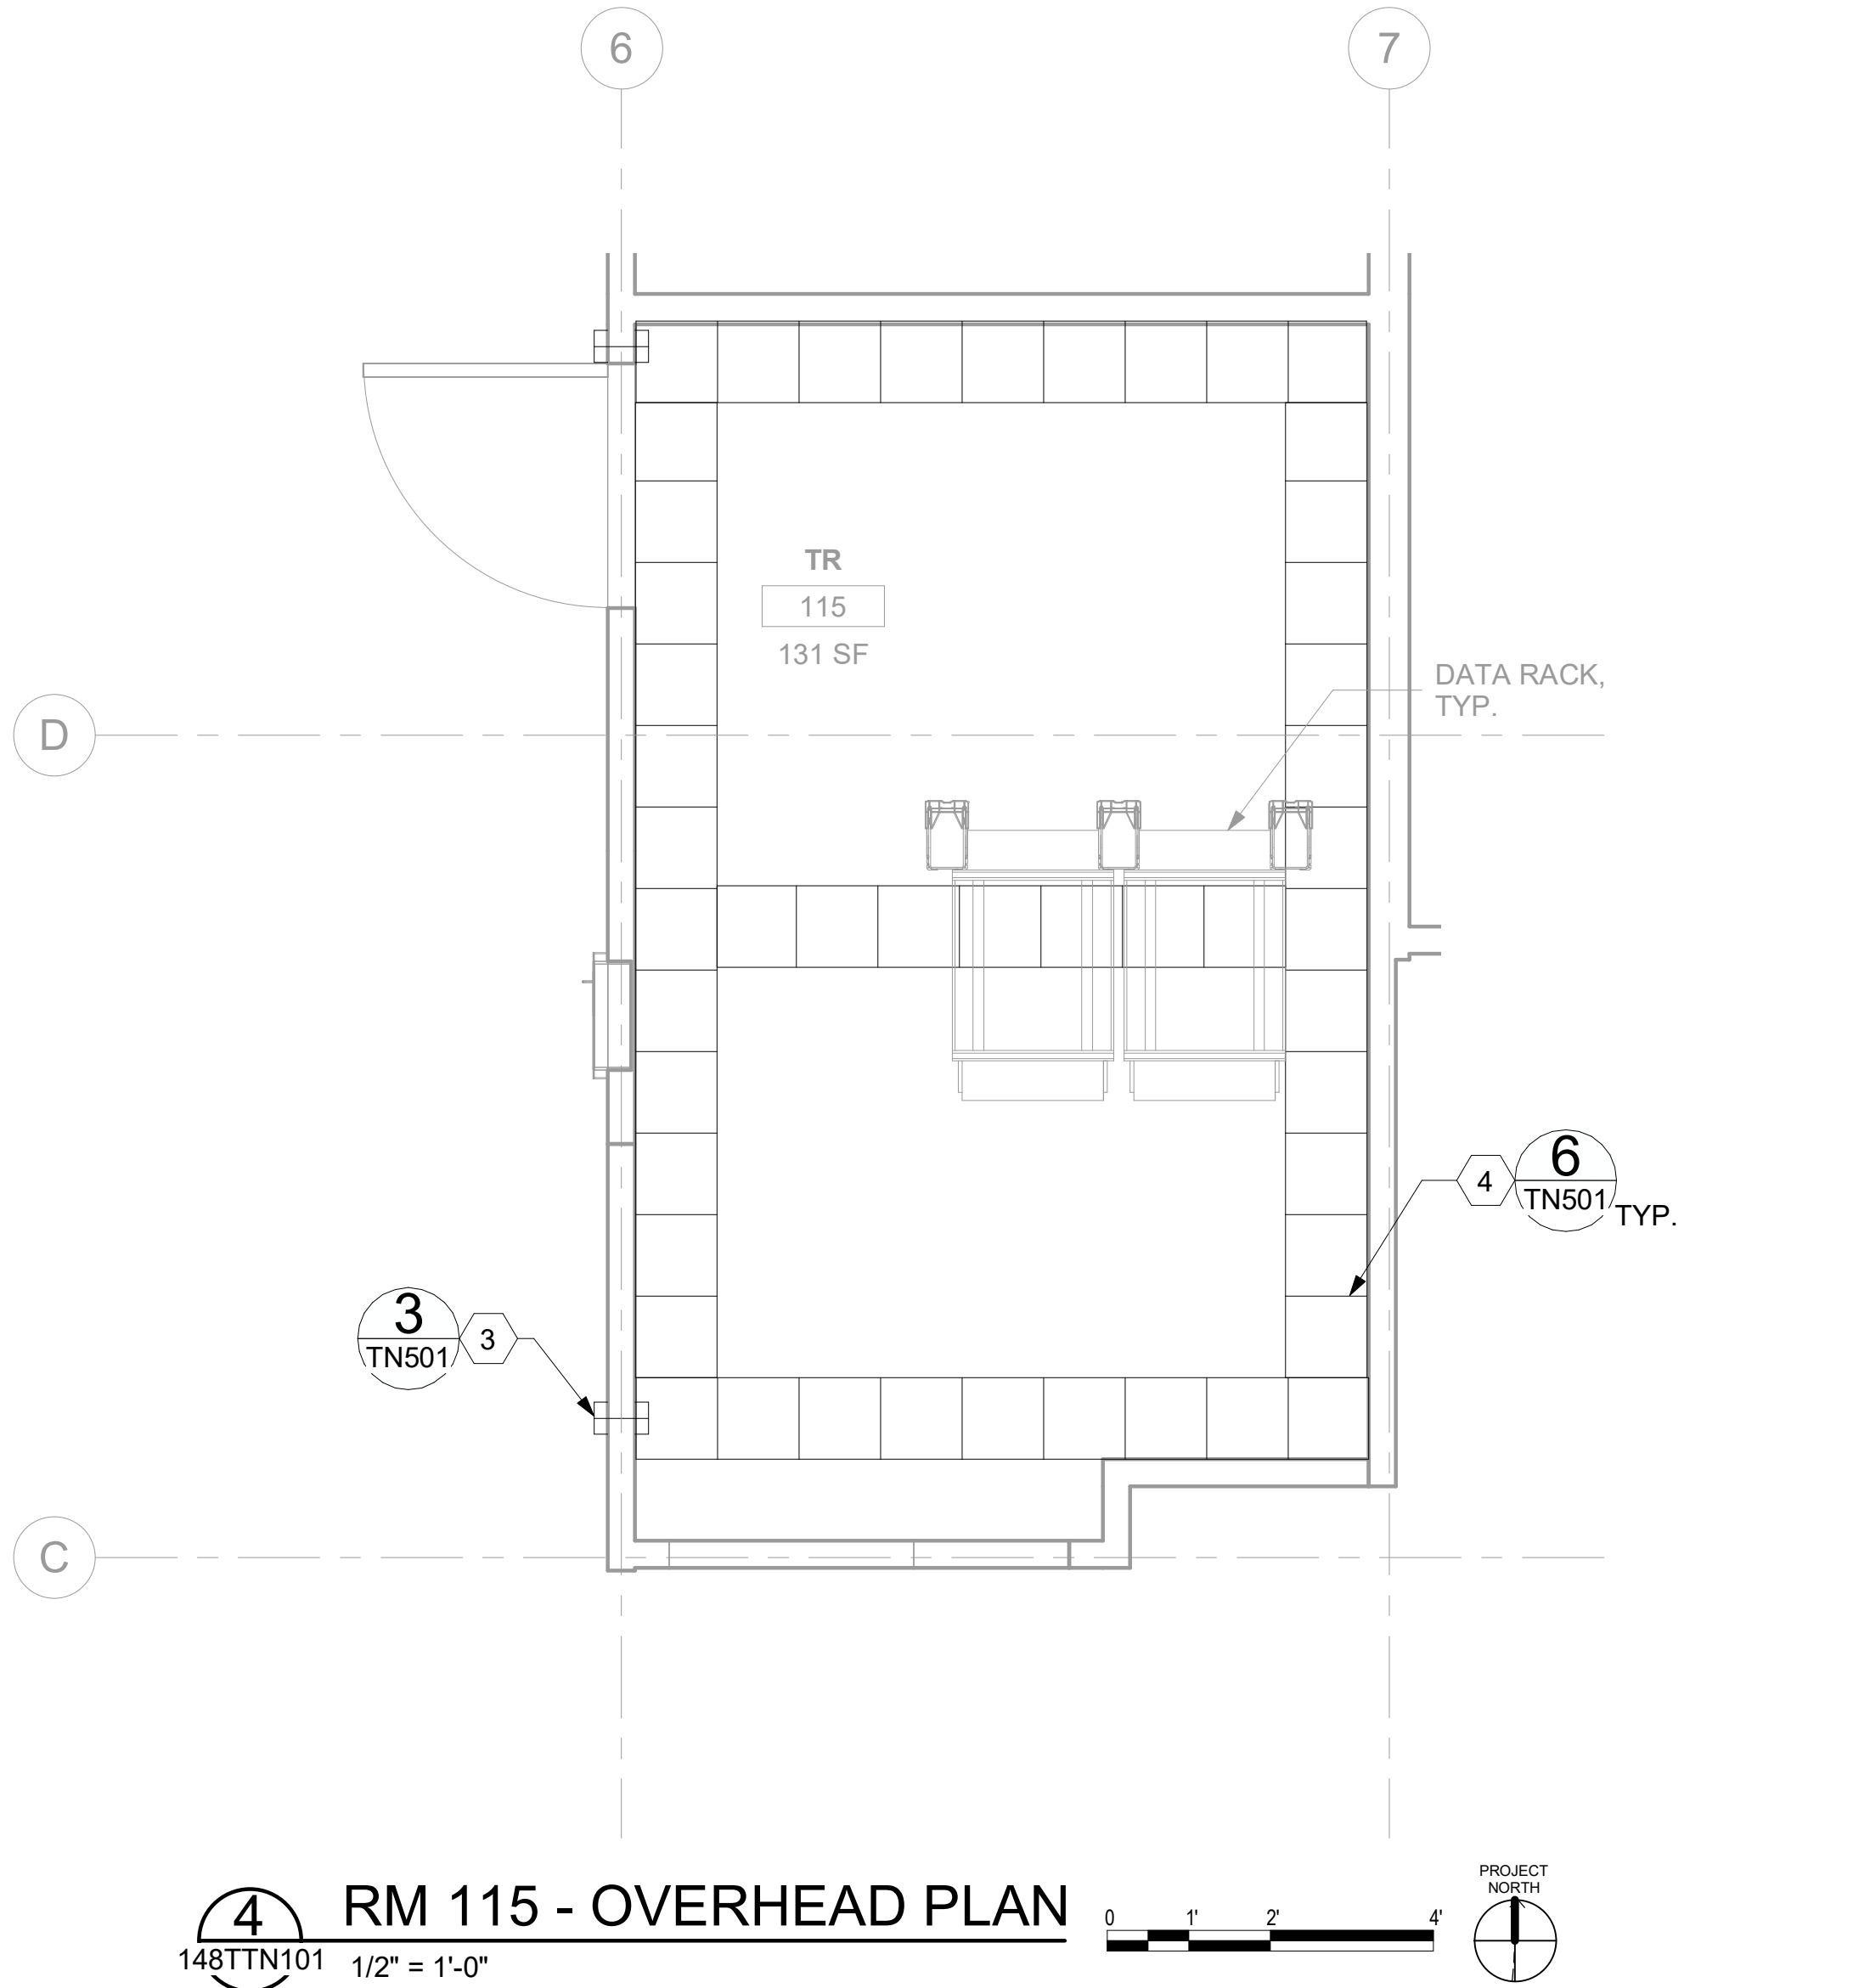

4 RM 115 - OVERHEAD PLAN

148TTN101 1/2" = 1'-0"

Revisions:	Date:

CONSULTANT
ENGINEERING DISCIPLINE:

ARCHITECT/ENGINEER OF RECORD
A/E:
SPEES DESIGN BUILD
23830 PACIFIC HIGHWAY S. SUITE 203
KENT, WA 98032


STAMP


Office of Construction and Facilities Management
 U.S. Department of Veterans Affairs

Drawing Title
BLDG 148T - LEVEL 01 - ENLARGED TELECOMMUNICATIONS PLANS
Approved:

Phase
100% CONSTRUCTION DOCUMENTS
FULLY SPRINKLERED

Project Title
EHRM INFRASTRUCTURE UPGRADES - HAMPTON
Location
HAMPTON VA MEDICAL CENTER, HAMPTON, VIRGINIA
Issue Date
07/18/2025
Checked
KG
Drawn
BCL/GPB

Project Number
590-22-700
Building Number
148T
Drawing Number
148TTN401
615 of 713

BLM 360/599-22-700
Washington EHRMEE - BLDG
168-11

15/07/2025 9:30:08 am


VA FORM 08 - 6231

3 RM 10 - DEMOLITION FLOOR PLAN
168TN100 NTS

BATTERY ROOM
10
954 SF


0 1' 2' 4'
PROJECT NORTH

2 RM 10B - TELECOMMUNICATIONS PLAN
168TN100 1/2" = 1'-0"

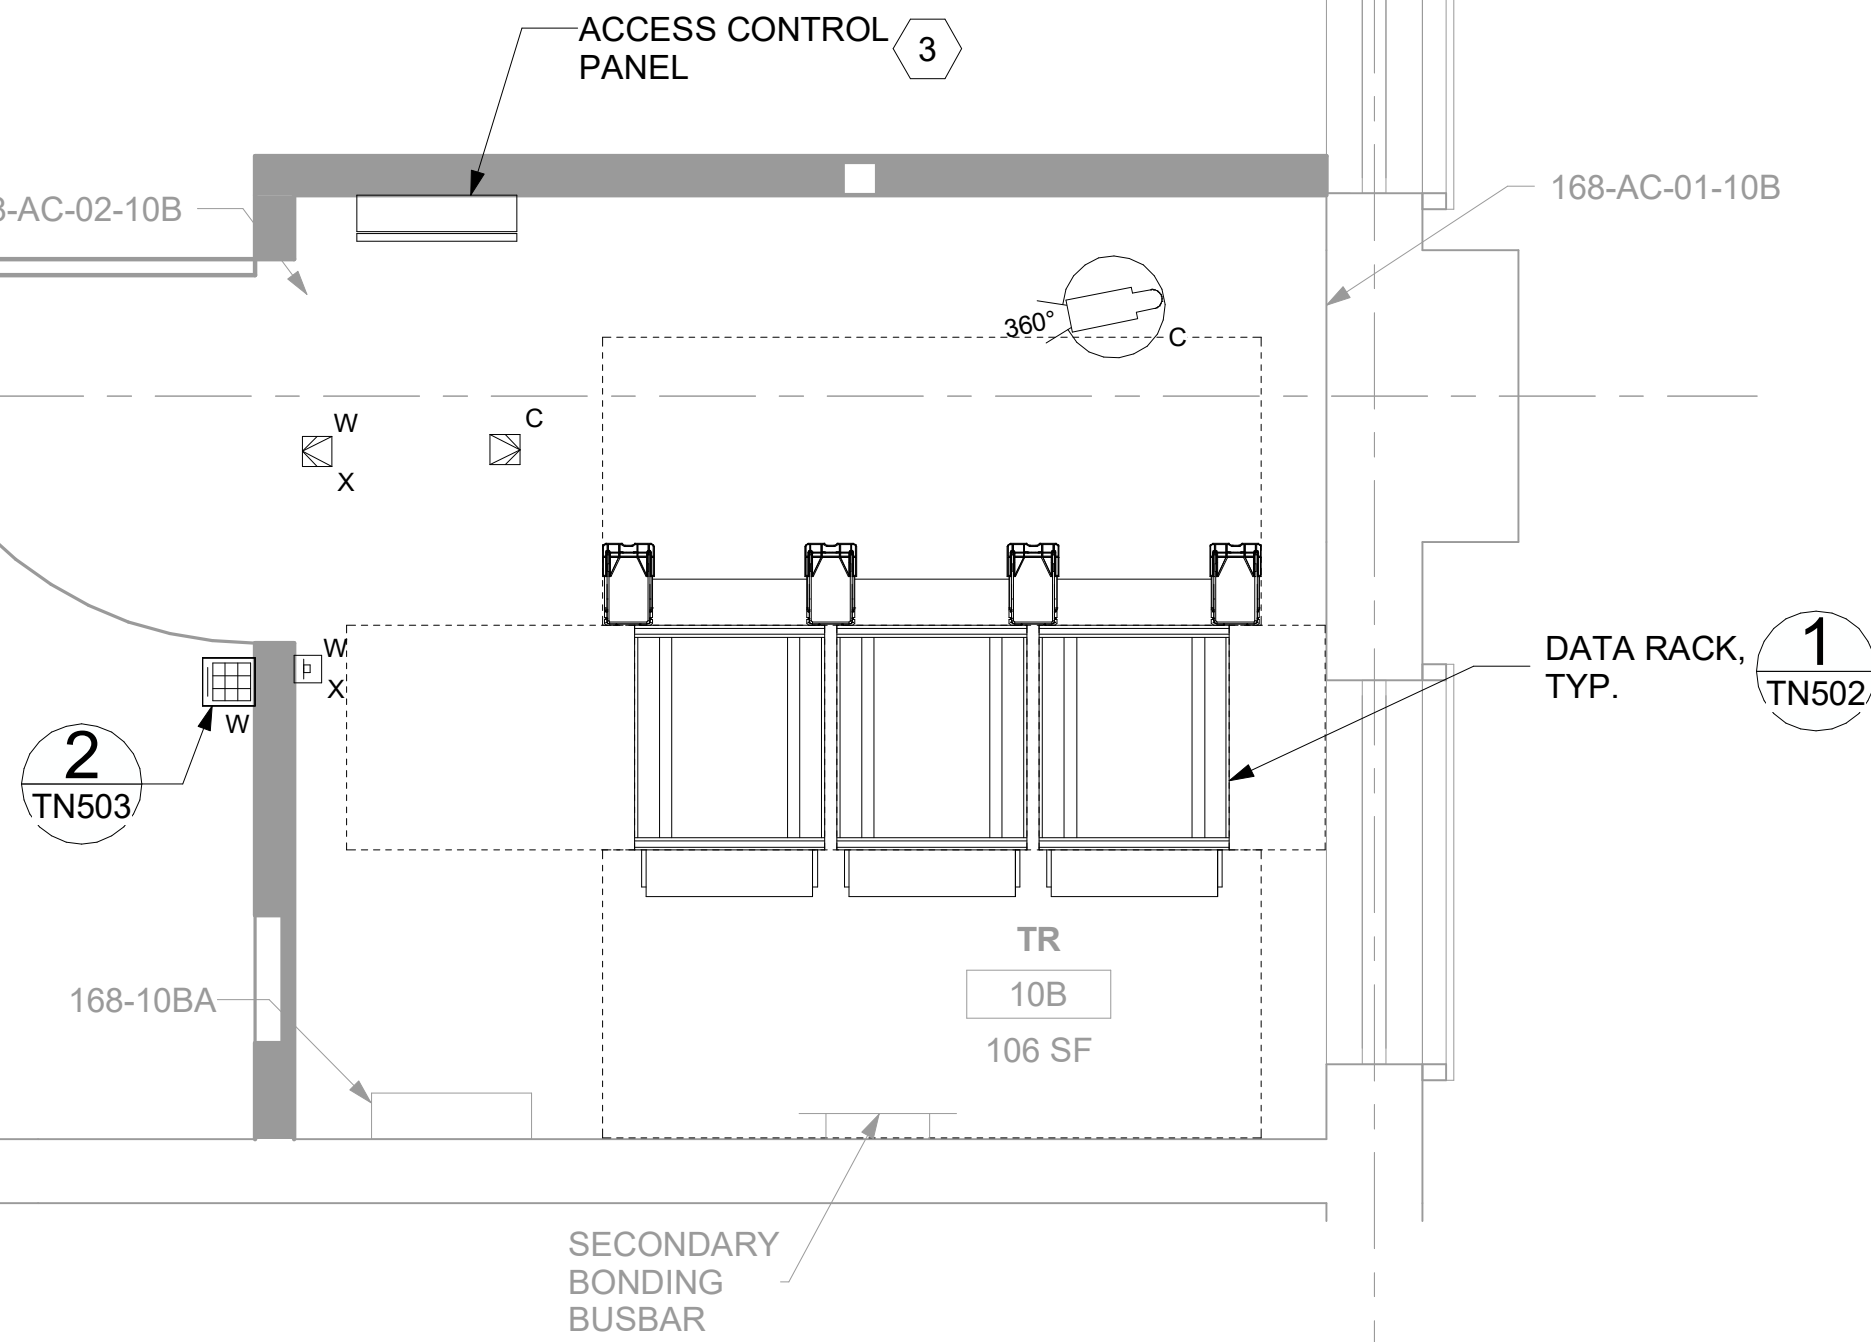

0 1' 2' 4'
PROJECT NORTH

4 RM 10B - OVERHEAD PLAN
168TN100 1/2" = 1'-0"

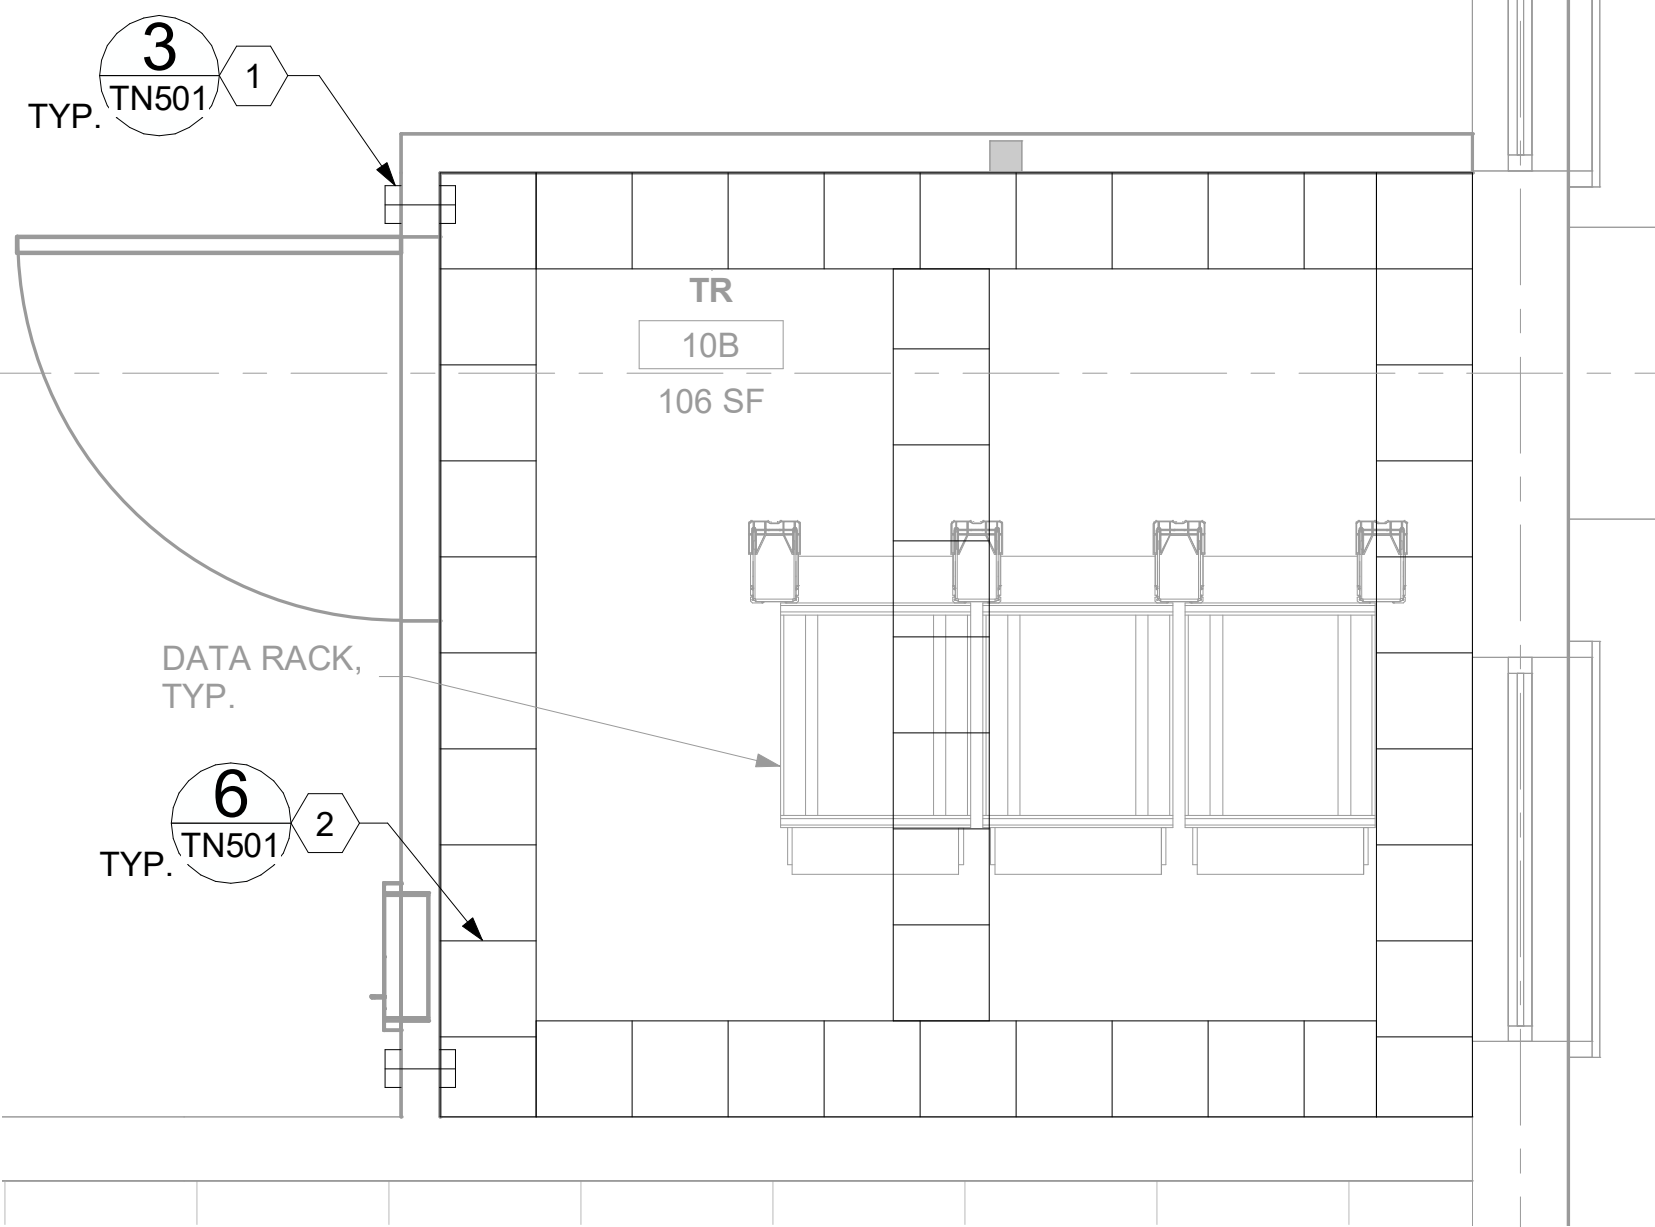

0 1' 2' 4'
PROJECT NORTH



GENERAL NOTES

- PROTECT ALL EXISTING WORK FROM DAMAGE DURING CONSTRUCTION. ANY DAMAGED MATERIALS, SYSTEMS, COMPONENTS, FINISHES AND THE LIKE, SHALL BE REPAIRED OR REPLACED AT THE EXPENSE OF THE CONTRACTOR TO THE ACCEPTANCE OF THE OWNER.
- SEAL ALL INTERIOR WALL AND CEILING PENETRATIONS TO MATCH EXISTING FIRE RATING OR NEW FIRE RATING, IF REQUIRED. COORDINATE WITH ARCHITECTURAL DRAWINGS AS REQUIRED.
- ALL TELECOMMUNICATIONS CABLING CATEGORY 6 AND BELOW SHALL BE REMOVED AND REPLACED WITH CAT6A PORTS AND CABLE QUANTITIES INDICATED, UNLESS NOTED OTHERWISE.
- TELECOMMUNICATIONS CABLES SHALL BE ROUTED IN EXISTING PATHWAY VACATED BY EXISTING CABLING. PROVIDE RACEWAYS TO EXTEND TO ASSOCIATED TR.
- A TELECOMMUNICATIONS OUTLET UPGRADE SHALL INCLUDE, BUT IS NOT LIMITED TO REMOVING AND DISPOSING EXISTING DEVICES AND CABLES; PROVIDING ALL LABOR, MATERIALS, TOOLS, TEST INSTRUMENTS, AND CONSUMABLES REQUIRED FOR THE INSTALLATION, TERMINATION, TESTING, LABELING, AND CERTIFICATION OF A FULLY FUNCTIONAL CATEGORY 6A OUTLET WITH THE PORT QUANTITY INDICATED.
- WHERE NEW DATA OUTLETS ARE BEING PROVIDED AND EXISTING DATA OUTLET CURRENTLY DOES NOT EXIST, PROVIDE (1) 1" CONDUIT FROM NEW BACKBOX TO ACCESSIBLE CEILING SPACE TO SECURELY ROUTE DATA CABLING FROM OUTLET TO TR VIA CABLE TRAY. IF CABLE TRAY IS NON-EXISTENT, EXTEND RACEWAY FROM OUTLET TO TR AS REQUIRED.
- PROVIDE CONDUITS AND SLEEVES AS REQUIRED FOR ROUTING AND INSTALLATION OF HORIZONTAL AND BACKBONE CABLING. PROVIDE FIRE-STOP MATERIALS TO SEAL IN AND AROUND CONDUIT PER CODE. REFER TO ARCHITECTURAL DRAWINGS FOR PARTITION TYPES AND WALL HEIGHTS.
- ALL TELECOMMUNICATION ROOMS SHALL BE PROVIDED WITH FIRE-RATED PLYWOOD BACKBOARDS. REFERENCE EXACT PLACEMENTS WITH ARCHITECTURE DRAWINGS AS REQUIRED.
- ANY LIVE SYSTEMS IN DEMO'D TR'S MUST REMAIN LIVE. CONTRACTOR TO COORDINATE WITH THE STATION TO IDENTIFY SYSTEMS THAT ARE LIVE. IF SYSTEMS ARE LIVE, INSTALL NEW CABLE FROM DEMO'D TR TO NEW TR. REFER TO DETAIL '3' ON TN506.
- RAIL KITS ARE PROVIDED BY THE GC FOR EQUIPMENT MOUNTED IN THE TR CHANNEL RACKS.
- LADDER RACK IN ALL TR'S WILL BE MOUNTED 6" OFF THE WALLS TO ACCOMMODATE ELECTRICAL AND MECHANICAL EQUIPMENT.

KEY NOTES

- PROVIDE RIGID CONDUIT SLEEVES WITH FIRE PROOFING AS REQUIRED. SIDE 'A' AND SIDE 'B' SLEEVES SHALL BE SEPARATED BY AT LEAST 10'-FT.
- WIRE BASKET CABLE TRAY.
- PROVIDE (2)-DOOR ACCESS CONTROL PANEL TO SERVE ALL PACS DOOR SECURITY EQUIPMENT FOR THIS TR ROOM. PROVIDE ALL REQUIRED CONNECTIONS, PROGRAMMING, POWER SUPPLIES, AND COMPONENTS TO PROVIDE A COMPLETE AND FULLY FUNCTIONAL SYSTEM. REFERENCE SPECIFICATION '28 13 00 -PHYSICAL ACCESS CONTROL SYSTEM' FOR ADDITIONAL INFORMATION.

KEY PLAN

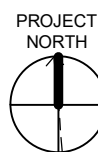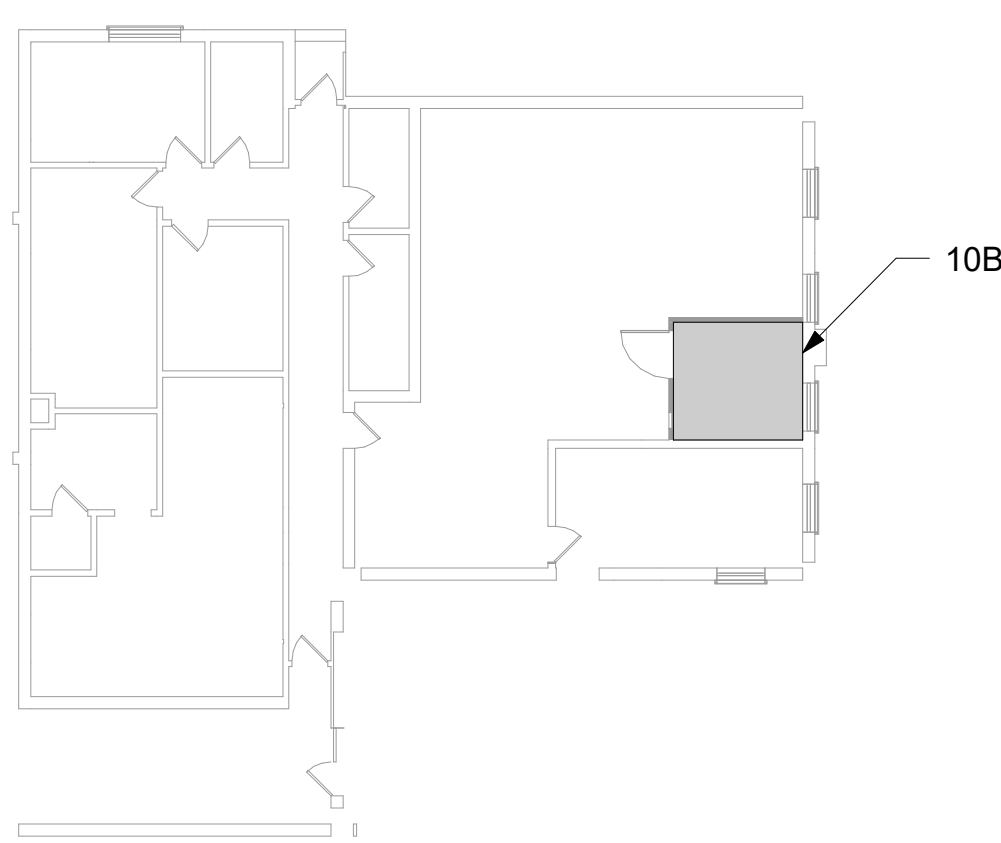

		CONSULTANT	ARCHITECT/ENGINEER OF RECORD	STAMP	Office of Construction and Facilities Management	Drawing Title	Phase	Project Title	Project Number	
		ENGINEERING DISCIPLINE:	A/E: SPEES DESIGN BUILD 23830 PACIFIC HIGHWAY S. SUITE 203 KENT, WA 98032			BLDG 168 - LEVEL 00 - ENLARGED TELECOMMUNICATIONS PLANS	100% CONSTRUCTION DOCUMENTS	EHRM INFRASTRUCTURE UPGRADES - HAMPTON	590-22-700	
						Approved:	FULLY SPRINKLERED	Location HAMPTON VA MEDICAL CENTER, HAMPTON, VIRGINIA	Building Number 168	
								Issue Date 07/18/2025	Checked KG	Drawn BCL/GPB
Revisions:	Date:				VA U.S. Department of Veterans Affairs				Drawing Number 168TN400 616 of 713	

OUTLET, DATA OR VOIP TELEPHONE. THE FOLLOWING INFORMATION INDICATED ON THE SYMBOL:
"N" = QUANTITY OF OUTLET PORTS.
"D" = EXISTING CABLES TO BE DEMOLISHED.
"N" = REPLACEMENT CABLES TO BE PROVIDED.
REFERENCE SHEET TNG002 FOR ADDITIONAL INFORMATION.


GENERAL NOTES

- PROTECT ALL EXISTING WORK FROM DAMAGE DURING CONSTRUCTION. ANY DAMAGED MATERIALS, SYSTEMS, COMPONENTS, FINISHES AND THE LIKE, SHALL BE REPAIRED OR REPLACED AT THE EXPENSE OF THE CONTRACTOR TO THE ACCEPTANCE OF THE OWNER.
- SEAL ALL INTERIOR WALL AND CEILING PENETRATIONS TO MATCH EXISTING FIRE RATING OR NEW FIRE RATING, IF REQUIRED. COORDINATE WITH ARCHITECTURAL DRAWINGS AS REQUIRED.
- ALL TELECOMMUNICATIONS CABLING CATEGORY 6 AND BELOW SHALL BE REMOVED AND REPLACED WITH CAT6A PORTS AND CABLE QUANTITIES INDICATED, UNLESS NOTED OTHERWISE.
- TELECOMMUNICATIONS CABLES SHALL BE ROUTED IN EXISTING PATHWAY VACATED BY EXISTING CABLING. PROVIDE RACEWAYS TO EXTEND TO ASSOCIATED TR.
- A TELECOMMUNICATIONS OUTLET UPGRADE SHALL INCLUDE, BUT IS NOT LIMITED TO REMOVING AND DISPOSING EXISTING DEVICES AND CABLES; PROVIDING ALL LABOR, MATERIALS, TOOLS, TEST INSTRUMENTS, AND CONSUMABLES REQUIRED FOR THE INSTALLATION, TERMINATION, TESTING, LABELING, AND CERTIFICATION OF A FULLY FUNCTIONAL CATEGORY 6A OUTLET WITH THE PORT QUANTITY INDICATED.
- WHERE NEW DATA OUTLETS ARE BEING PROVIDED AND EXISTING DATA OUTLET CURRENTLY DOES NOT EXIST, PROVIDE (1) 1" CONDUIT FROM NEW BACKBOX TO ACCESSIBLE CEILING SPACE TO SECURELY ROUTE DATA CABLING FROM OUTLET TO TR VIA CABLE TRAY. IF CABLE TRAY IS NON-EXISTENT, EXTEND RACEWAY FROM OUTLET TO TR AS REQUIRED.
- PROVIDE CONDUITS AND SLEEVES AS REQUIRED FOR ROUTING AND INSTALLATION OF HORIZONTAL AND BACKBONE CABLING. PROVIDE FIRE-STOP MATERIALS TO SEAL IN AND AROUND CONDUIT PER CODE. REFER TO ARCHITECTURAL DRAWINGS FOR PARTITION TYPES AND WALL HEIGHTS.
- ALL TELECOMMUNICATION ROOMS SHALL BE PROVIDED WITH FIRE-RATED PLYWOOD BACKBOARDS. REFERENCE EXACT PLACEMENTS WITH ARCHITECTURE DRAWINGS AS REQUIRED.
- ANY LIVE SYSTEMS IN DEMO'D TR'S MUST REMAIN LIVE. CONTRACTOR TO COORDINATE WITH THE STATION TO IDENTIFY SYSTEMS THAT ARE LIVE. IF SYSTEMS ARE LIVE, INSTALL NEW CABLE FROM DEMO'D TR TO NEW TR. REFER TO DETAIL '3' ON TN506.
- RAIL KITS ARE PROVIDED BY THE GC FOR EQUIPMENT MOUNTED IN THE TR CHANNEL RACKS.
- LADDER RACK IN ALL TR'S WILL BE MOUNTED 6" OFF THE WALLS TO ACCOMMODATE ELECTRICAL AND MECHANICAL EQUIPMENT.

KEY NOTES

- EXISTING DATA RACK TO BE DECOMMISSIONED BY VA. CONTRACTOR SHALL COORDINATE WITH VA AS REQUIRED.
- WIRE BASKET CABLE TRAY.
- EXISTING VERTICAL CABLING SLEEVE TO BE PRESERVED. EXISTING FIBER OPTIC AND/OR EXISTING VERTICAL CABLING RELATED TO EXISTING TR RACKS TO BE DEMOLISHED.
- EXISTING HORIZONTAL CABLING SLEEVE TO BE PRESERVED. EXISTING FIBER OPTIC AND/OR EXISTING HORIZONTAL CABLING RELATED TO EXISTING TR RACKS TO BE DEMOLISHED.
- EXISTING CABLE TRAY TO BE DEMOLISHED AND REMOVED.
- EXISTING CCTV TO BE RELOCATED.
- PROVIDE RIGID CONDUIT SLEEVES WITH FIRE PROOFING AS REQUIRED. SIDE 'A' AND SIDE 'B' SLEEVES SHALL BE SEPARATED BY ATLEAST 10FT.
- EXISTING ACCESS CONTROL PANEL TO BE MODIFIED TO PROVIDE ALL REQUIRED CONNECTIONS AND HARDWARE FOR MOTION DETECTOR.
- PROVIDE (2)-DOOR ACCESS CONTROL PANEL TO SERVE ALL PACS DOOR SECURITY EQUIPMENT FOR THIS TR ROOM. PROVIDE ALL REQUIRED CONNECTIONS, PROGRAMMING, POWER SUPPLIES, AND COMPONENTS TO PROVIDE A COMPLETE AND FULLY FUNCTIONAL SYSTEM. REFERENCE SPECIFICATION "28 13 00 - PHYSICAL ACCESS CONTROL SYSTEM" FOR ADDITIONAL INFORMATION.
- EXISTING ACCESS CONTROL PANEL TO BE RE-FED WITH (1) CAT6A CABLE.
- EXISTING EQUIPMENT TO BE DEMOLISHED. ASSOCIATED RACEWAYS AND CABLING SHALL BE DEMOLISHED BACK TO SOURCE.
- PROVIDE TELECOMMUNICATIONS OUTLET WITH PORT QUANTITY SHOWN TO REPLACE EXISTING TELECOMMUNICATIONS OUTLET; EXISTING OUTLET CONDUIT SHALL REMAIN AND BE UTILIZED TO FEED NEW CABLING; REFERENCE DETAIL '1' ON SHEET TN501 AND THE GENERAL NOTES ON THIS SHEET FOR ADDITIONAL INFORMATION. COORDINATE WITH VA FOR EXACT OUTLET PLACEMENT.
- EXISTING WIRELESS ACCESS POINT TO BE RE-FED WITH (2) CAT6A CABLES.

KEY PLAN

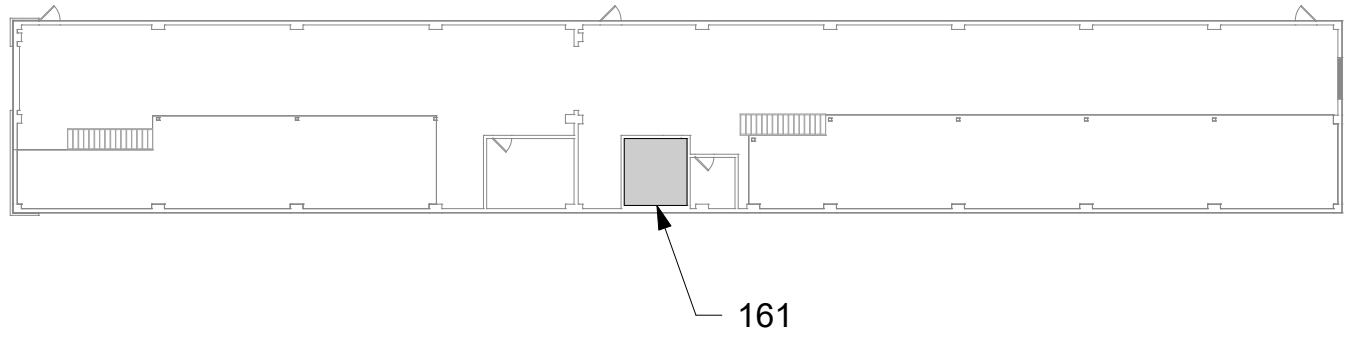

AREA SHOWN

1 RM 161 - DEMOLITION FLOOR PLAN

173&173ATN101 1/2" = 1'-0"

2 RM 161 - TELECOMMUNICATIONS PLAN

173&173ATN101 1/2" = 1'-0"




3 RM 161 - DEMOLITION OVERHEAD PLAN

173&173ATN101 1/2" = 1'-0"

4 RM 161 - OVERHEAD PLAN




173&173ATN101 1/2" = 1'-0"

		CONSULTANT	ARCHITECT/ENGINEER OF RECORD	STAMP	Office of Construction and Facilities Management VA U.S. Department of Veterans Affairs	Drawing Title	Phase	Project Title	Project Number
		ENGINEERING DISCIPLINE:	A/E: SPEES DESIGN BUILD 23830 PACIFIC HIGHWAY S. SUITE 203 KENT, WA 98032			BLDG 173 & 173A - LEVEL 01 - ENLARGED TELECOMMUNICATIONS PLANS	100% CONSTRUCTION DOCUMENTS	EHRM INFRASTRUCTURE UPGRADES - HAMPTON	590-22-700
						Approved:	FULLY SPRINKLERED	Location HAMPTON VA MEDICAL CENTER, HAMPTON, VIRGINIA	Building Number 173 & 173A
		Revisions:	Date:					Issue Date 07/18/2025	Drawing Number 173&173ATN401
								Checked KG	617 of 713
								Drawn BCL/GPB	

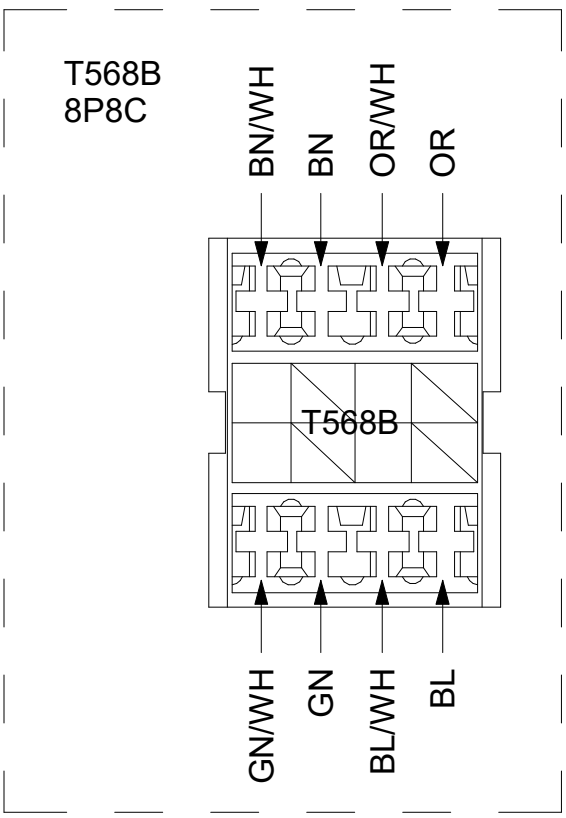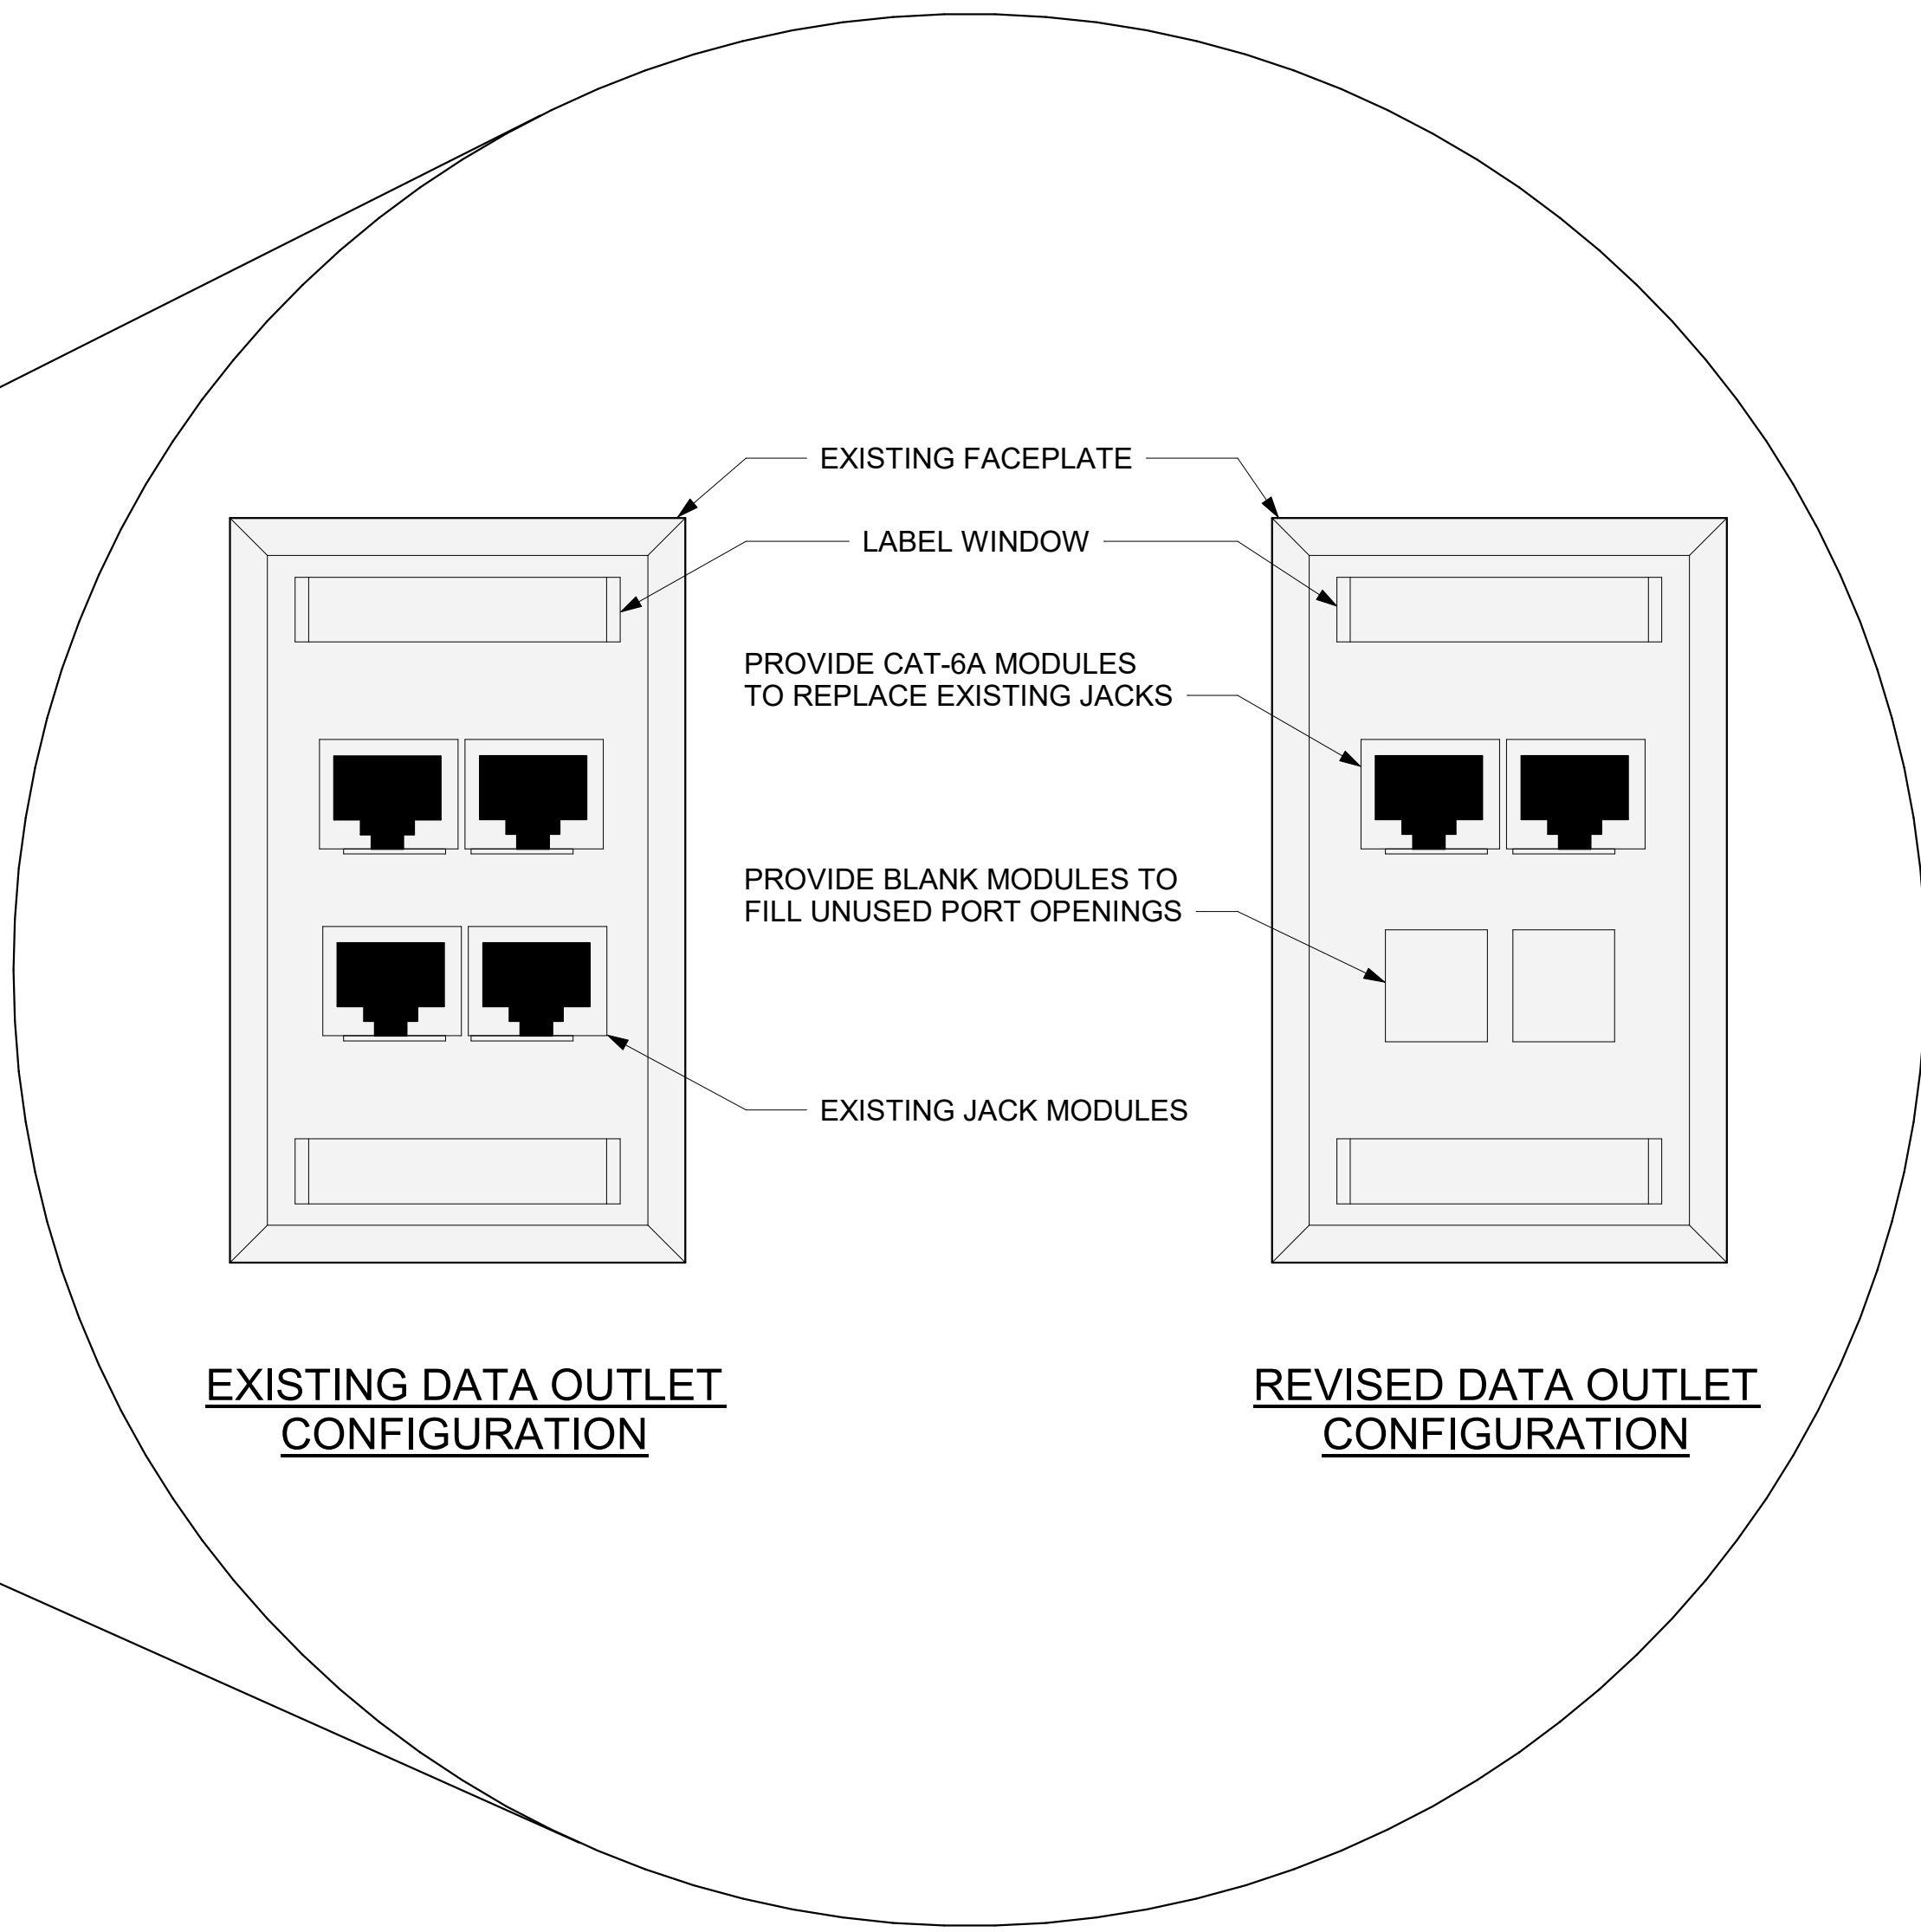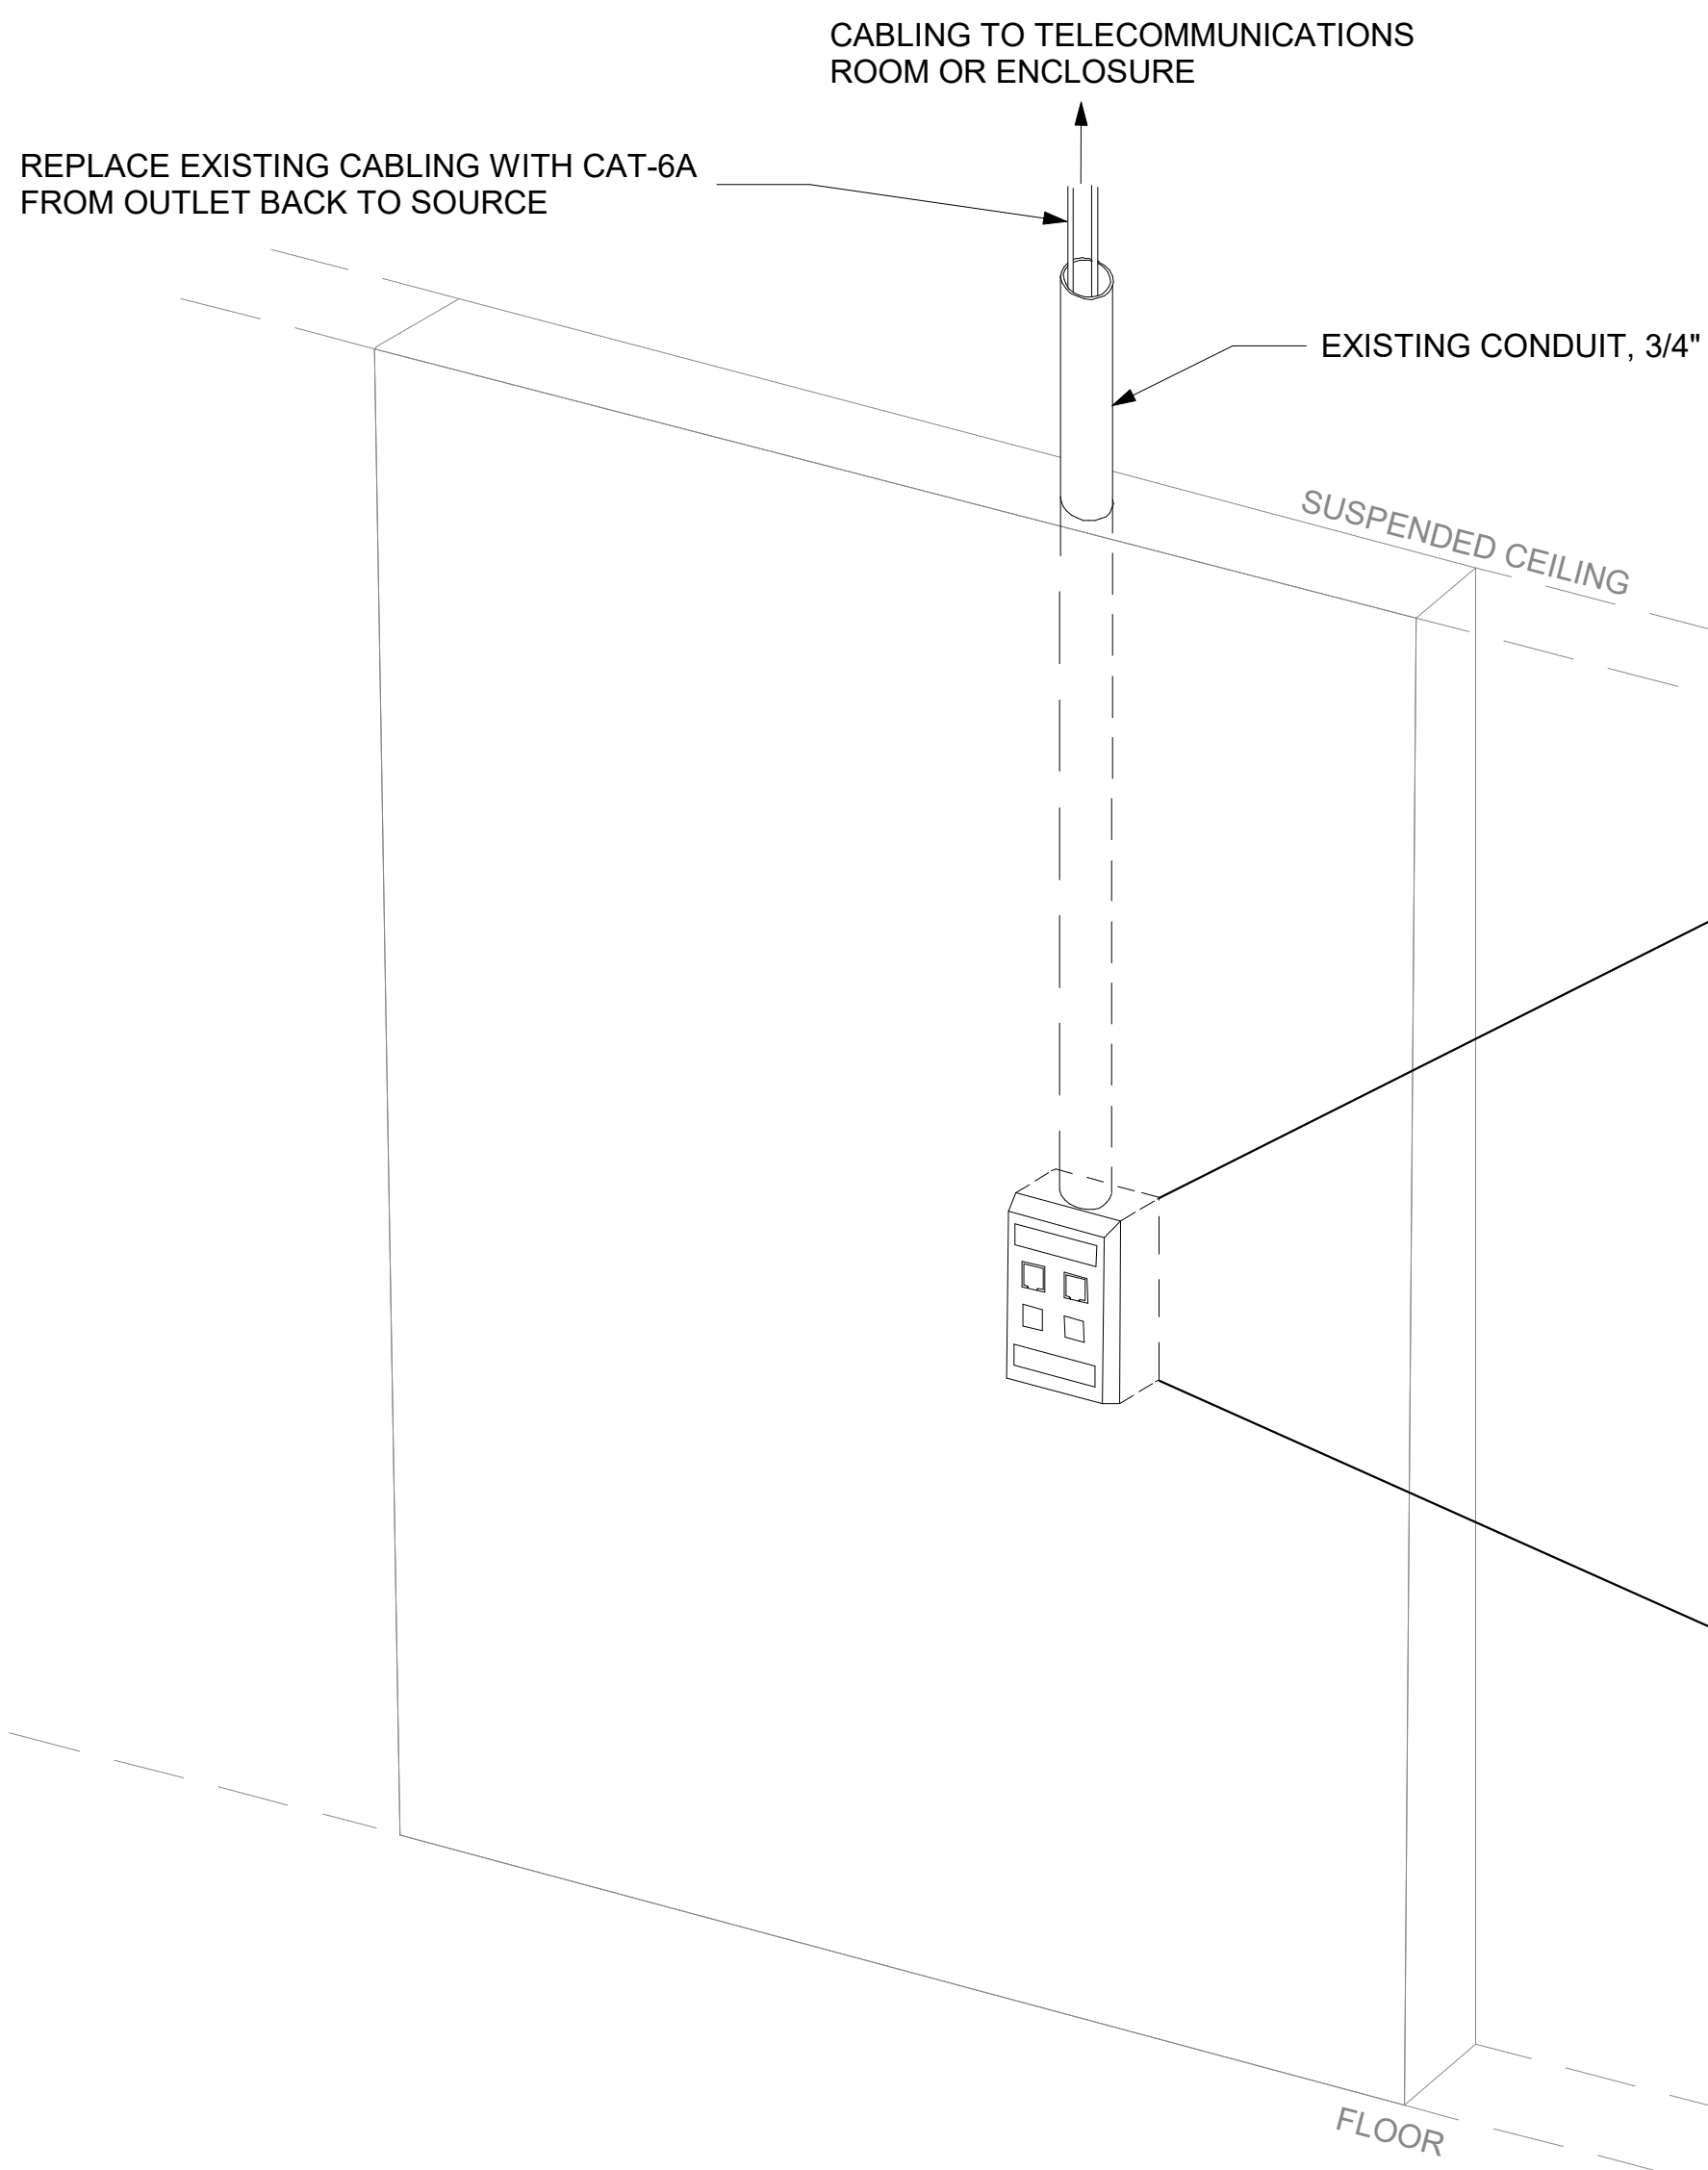

1 EXISTING CONDUIT WITH CABLING MODIFICATION SECTION VIEW
- NTS

2 DATA CABLING TERMINATION DETAIL
- NTS

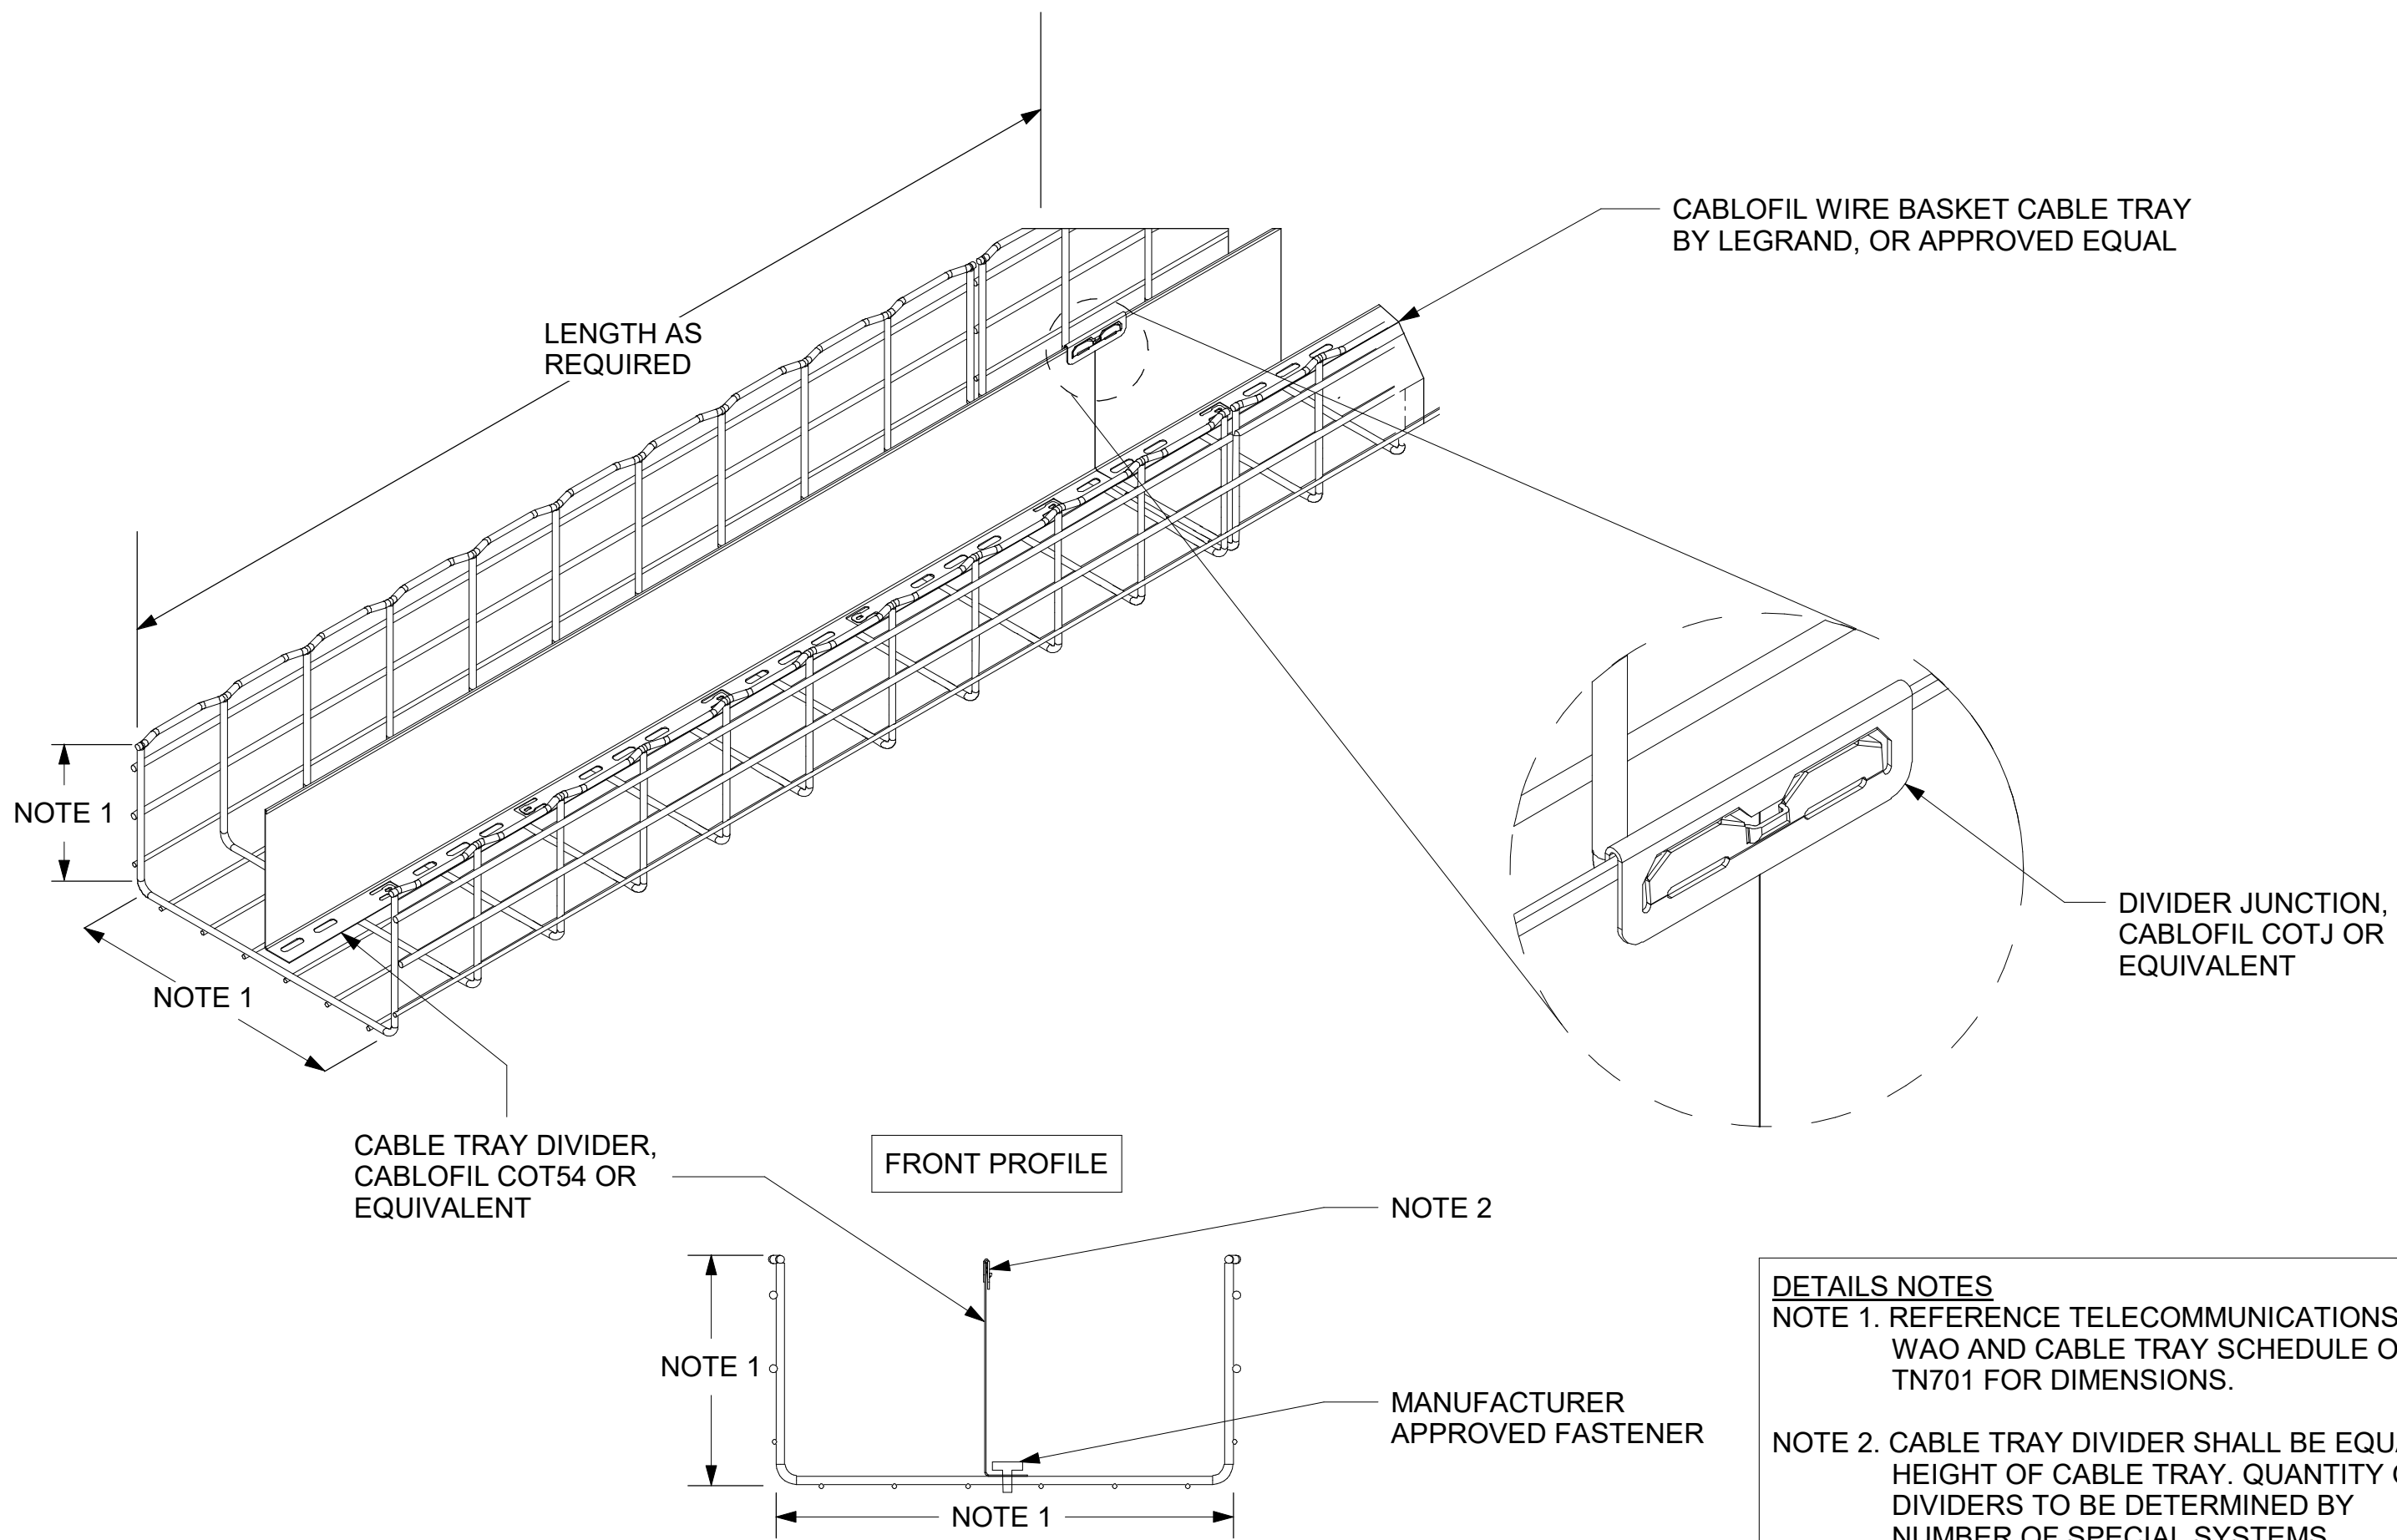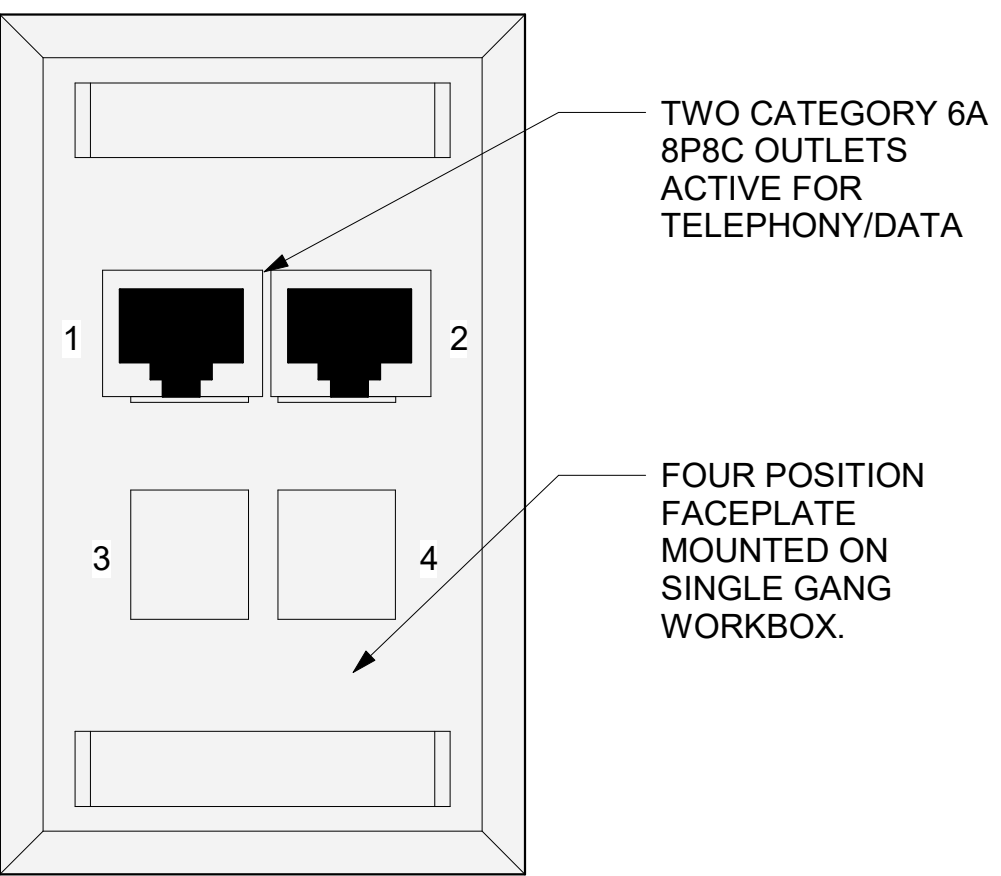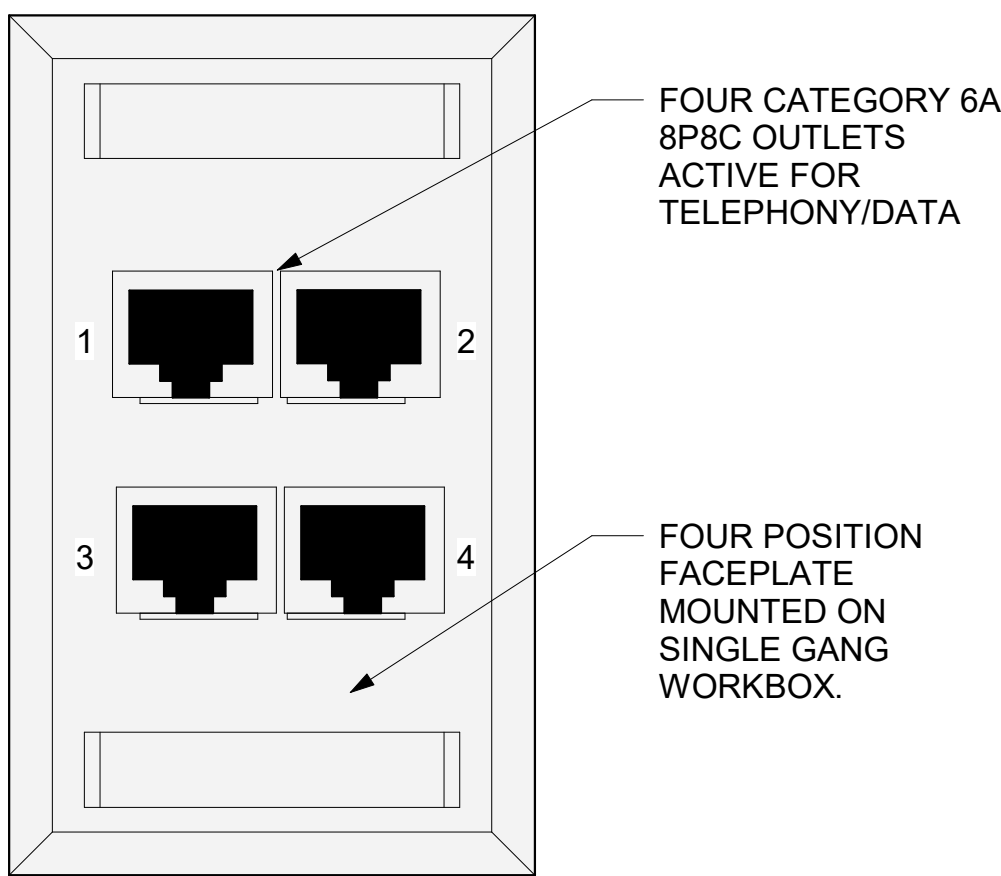

DETAILS NOTES
NOTE 1. REFERENCE TELECOMMUNICATIONS WAO AND CABLE TRAY SCHEDULE ON TN701 FOR DIMENSIONS.
NOTE 2. CABLE TRAY DIVIDER SHALL BE EQUAL HEIGHT OF CABLE TRAY. QUANTITY OF DIVIDERS TO BE DETERMINED BY NUMBER OF SPECIAL SYSTEMS ROUTED THROUGH CABLE TRAY. CONTRACTOR SHALL ASSUME A MINIMUM OF 4 DIVIDERS PER TRAY.
NOTE 3. CABLE TRAY SHALL BE INSTALLED 6" OFF WALL TO ALLOW CONDUIT TO PASS BEHIND TRAY.

3 TYPICAL FIRE STOP SLEEVE DETAIL
- NTS

4 TYPICAL HIGH DENSITY WALL MOUNTED WORK AREA OUTLET CONFIGURATION
- NTS


5 STANDARD DENSITY WALL MOUNTED WORK AREA OUTLET CONFIGURATION
- NTS

6 WIRE BASKET CABLE TRAY WITH DIVIDER
- NTS

Revisions:	Date:

CONSULTANT
ENGINEERING DISCIPLINE:

ARCHITECT/ENGINEER OF RECORD
A/E:
SPEES DESIGN BUILD
23830 PACIFIC HIGHWAY S. SUITE 203
KENT, WA 98032
SDE SPEEDDESIGNBUILD

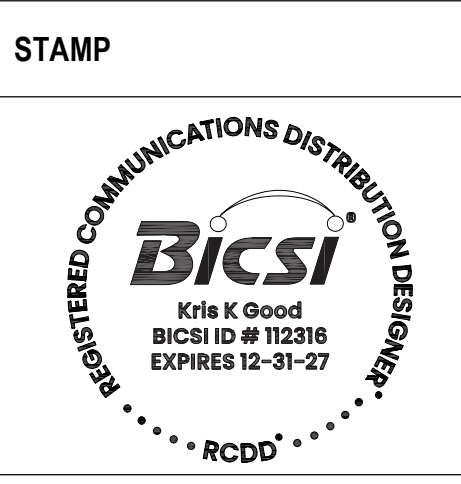

Office of Construction and Facilities Management
VA U.S. Department of Veterans Affairs

Drawing Title
TELECOMMUNICATIONS DETAILS
Approved:

Phase
100% CONSTRUCTION DOCUMENTS
FULLY SPRINKLERED

Project Title
EHRM INFRASTRUCTURE UPGRADES - HAMPTON
Location
HAMPTON VA MEDICAL CENTER, HAMPTON, VIRGINIA
Issue Date
07/18/2025
Checked
KG
Drawn
BCL/GPB

Project Number
590-22-700
Building Number
-
Drawing Number
TN501
618 of 713


BVA 3601/599-22-700
Validation EHRMVA
General
Notes, Diagrams and Details V15
15/07/2025 8:36:02 am

VA FORM 08 - 6231


GENERAL NOTES (FOR THIS SHEET ONLY)

- ALL TELECOMMUNICATIONS ROOM (TR) DATA RACK DETAIL ELEVATIONS ARE SHOWN TO PROVIDE GENERAL LAYOUT REQUIREMENTS. EXACT QUANTITIES OF UTP PATCH PANELS AND NETWORK SWITCHES PER TR ARE SHOWN IN THE TELECOMMUNICATIONS WAO AND CABLE TRAY SCHEDULE LOCATED ON SHEET TN701. IF MORE THAN (1) RACK IS PRESENT IN THE TR BEING EVALUATED, CONTRACTOR SHALL DIVIDE THE PATCH PANEL AND NETWORK SWITCH EQUIPMENT EVENLY AMONG THE RACKS (IE: IF (6) PATCH PANELS AND (6) NETWORK SWITCHES ARE REQUIRED IN A TR THAT HAS (2) DATA RACKS, PROVIDE EACH DATA RACK WITH (3) PATCH PANELS AND (3) NETWORK SWITCHES).
- VA DATA RACKS FOLLOW A RULE OF THIRDS FOR POSITIONING EQUIPMENT ON THE RACK. THE TOP THIRD IS DESIGNATED FOR FIBER AND UTP PATCH EQUIPMENT, THE MIDDLE THIRD IS DESIGNATED FOR NETWORK SWITCH EQUIPMENT, AND THE BOTTOM THIRD IS DESIGNATED FOR DATA RACK POWER DISTRIBUTION EQUIPMENT.
- PRIOR TO CONSTRUCTING TR DATA RACKS AND DURING THE SUBMITTAL PROCESS, CONTRACTOR SHALL SUBMIT ALL TR DATA RACK ELEVATIONS (FRONT, BACK, AND SIDE VIEWS) FOR ENGINEER AND VA REVIEW AND APPROVAL. SUBMITTAL SHALL SHOW ALL DIMENSIONS, CABLE MANAGEMENT EQUIPMENT, LABELING AND ASSOCIATED CUTSHEETS WITH INDICATED PART NUMBERS AND OPTIONS FOR ALL EQUIPMENT.
- CONTRACTOR SHALL LABEL EACH PATCH PANEL PORT WITH PORT NUMBER AND ROOM NUMBER.
- ALL DATA RACKS SHALL BE PROVIDED WITH SEISMIC BRACING KITS AND INSTALLED PER MANUFACTURER'S INSTRUCTIONS.
- ALL EQUIPMENT, CABLING, CONNECTORS AND APPURTENANCES SHALL BE LABELED PER THE VA STANDARD "INFRASTRUCTURE STANDARD FOR TELECOMMUNICATIONS SPACE" VERSION 3.1 OR NEWER.
- WHERE RACK EQUIPMENT IS NOT REQUIRED FOR CABLING REQUIREMENTS PROVIDE BLANKING PANELS IN ABSENT SPACES.
- PROVIDE BLANKING PANELS IN ALL TR RACK VACANT SPACES IF NOT NOTED OTHERWISE.

DETAIL IS GENERIC IN NATURE AND SHOWS GENERAL LAYOUT INFORMATION.
REFERENCE GENERAL AND KEY NOTES FOR SPECIFIC INFORMATION

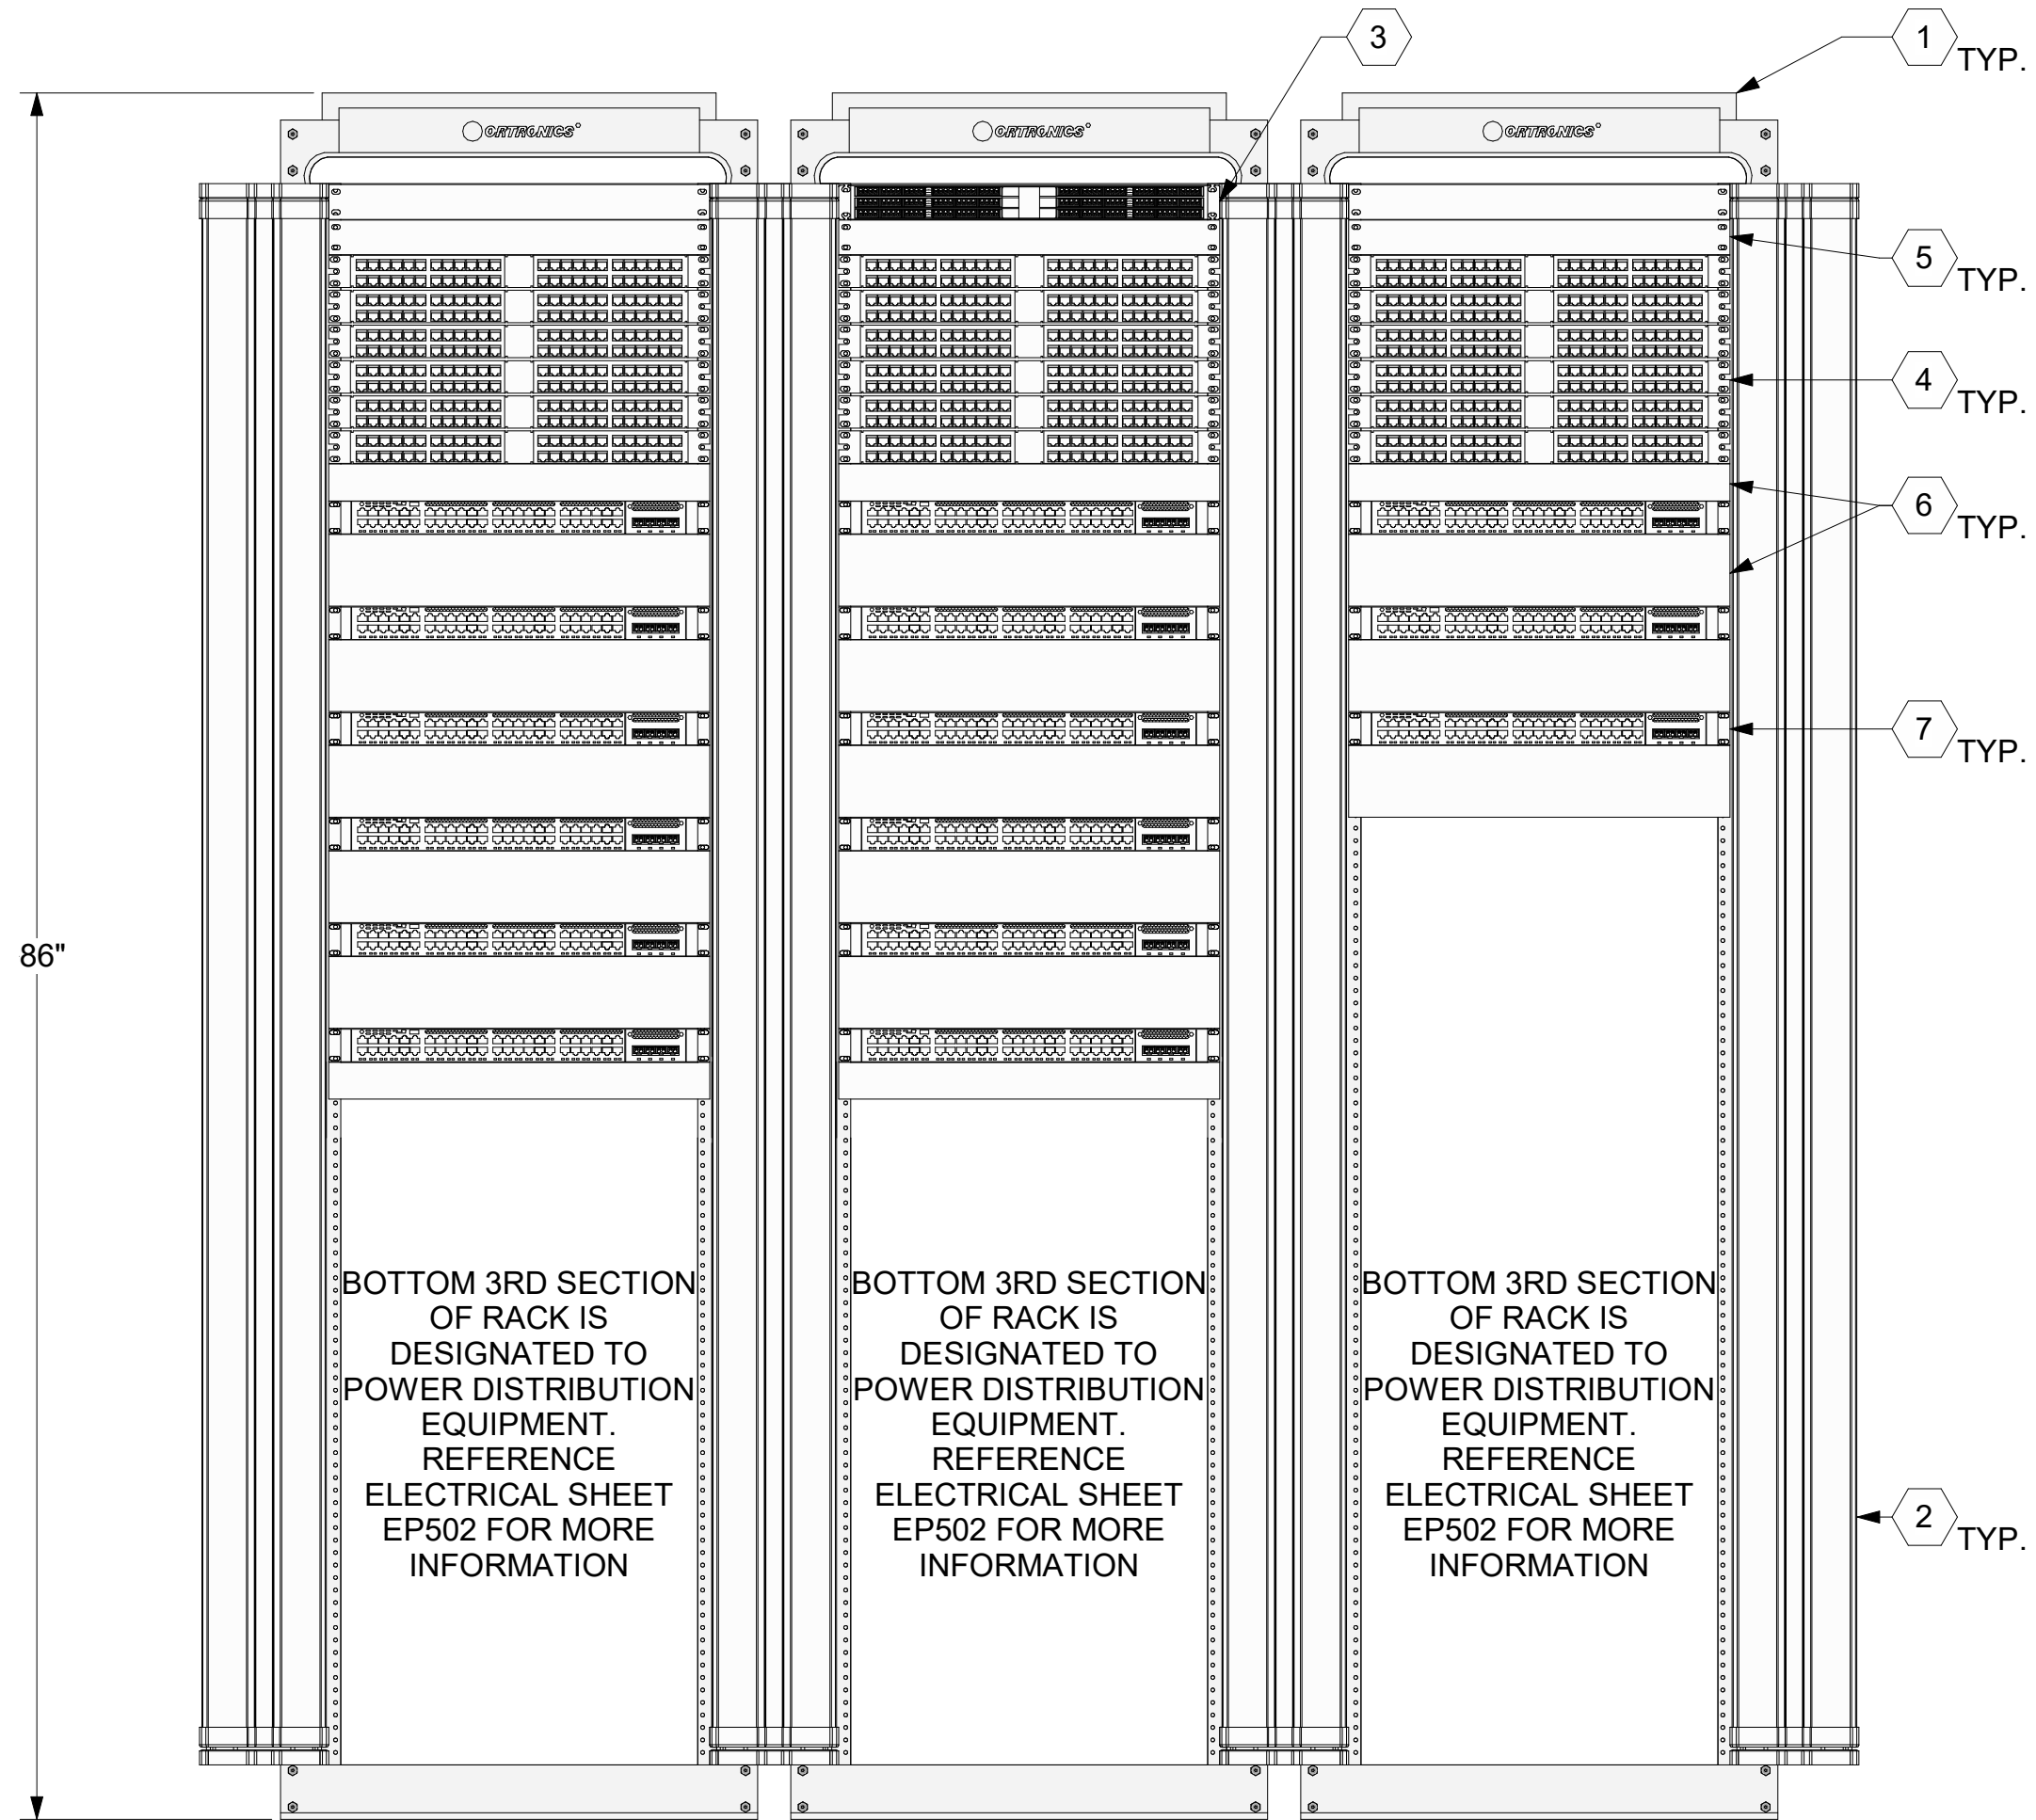


1 TR DATA RACK ELEVATION - THREE RACK
1" = 0'-9"

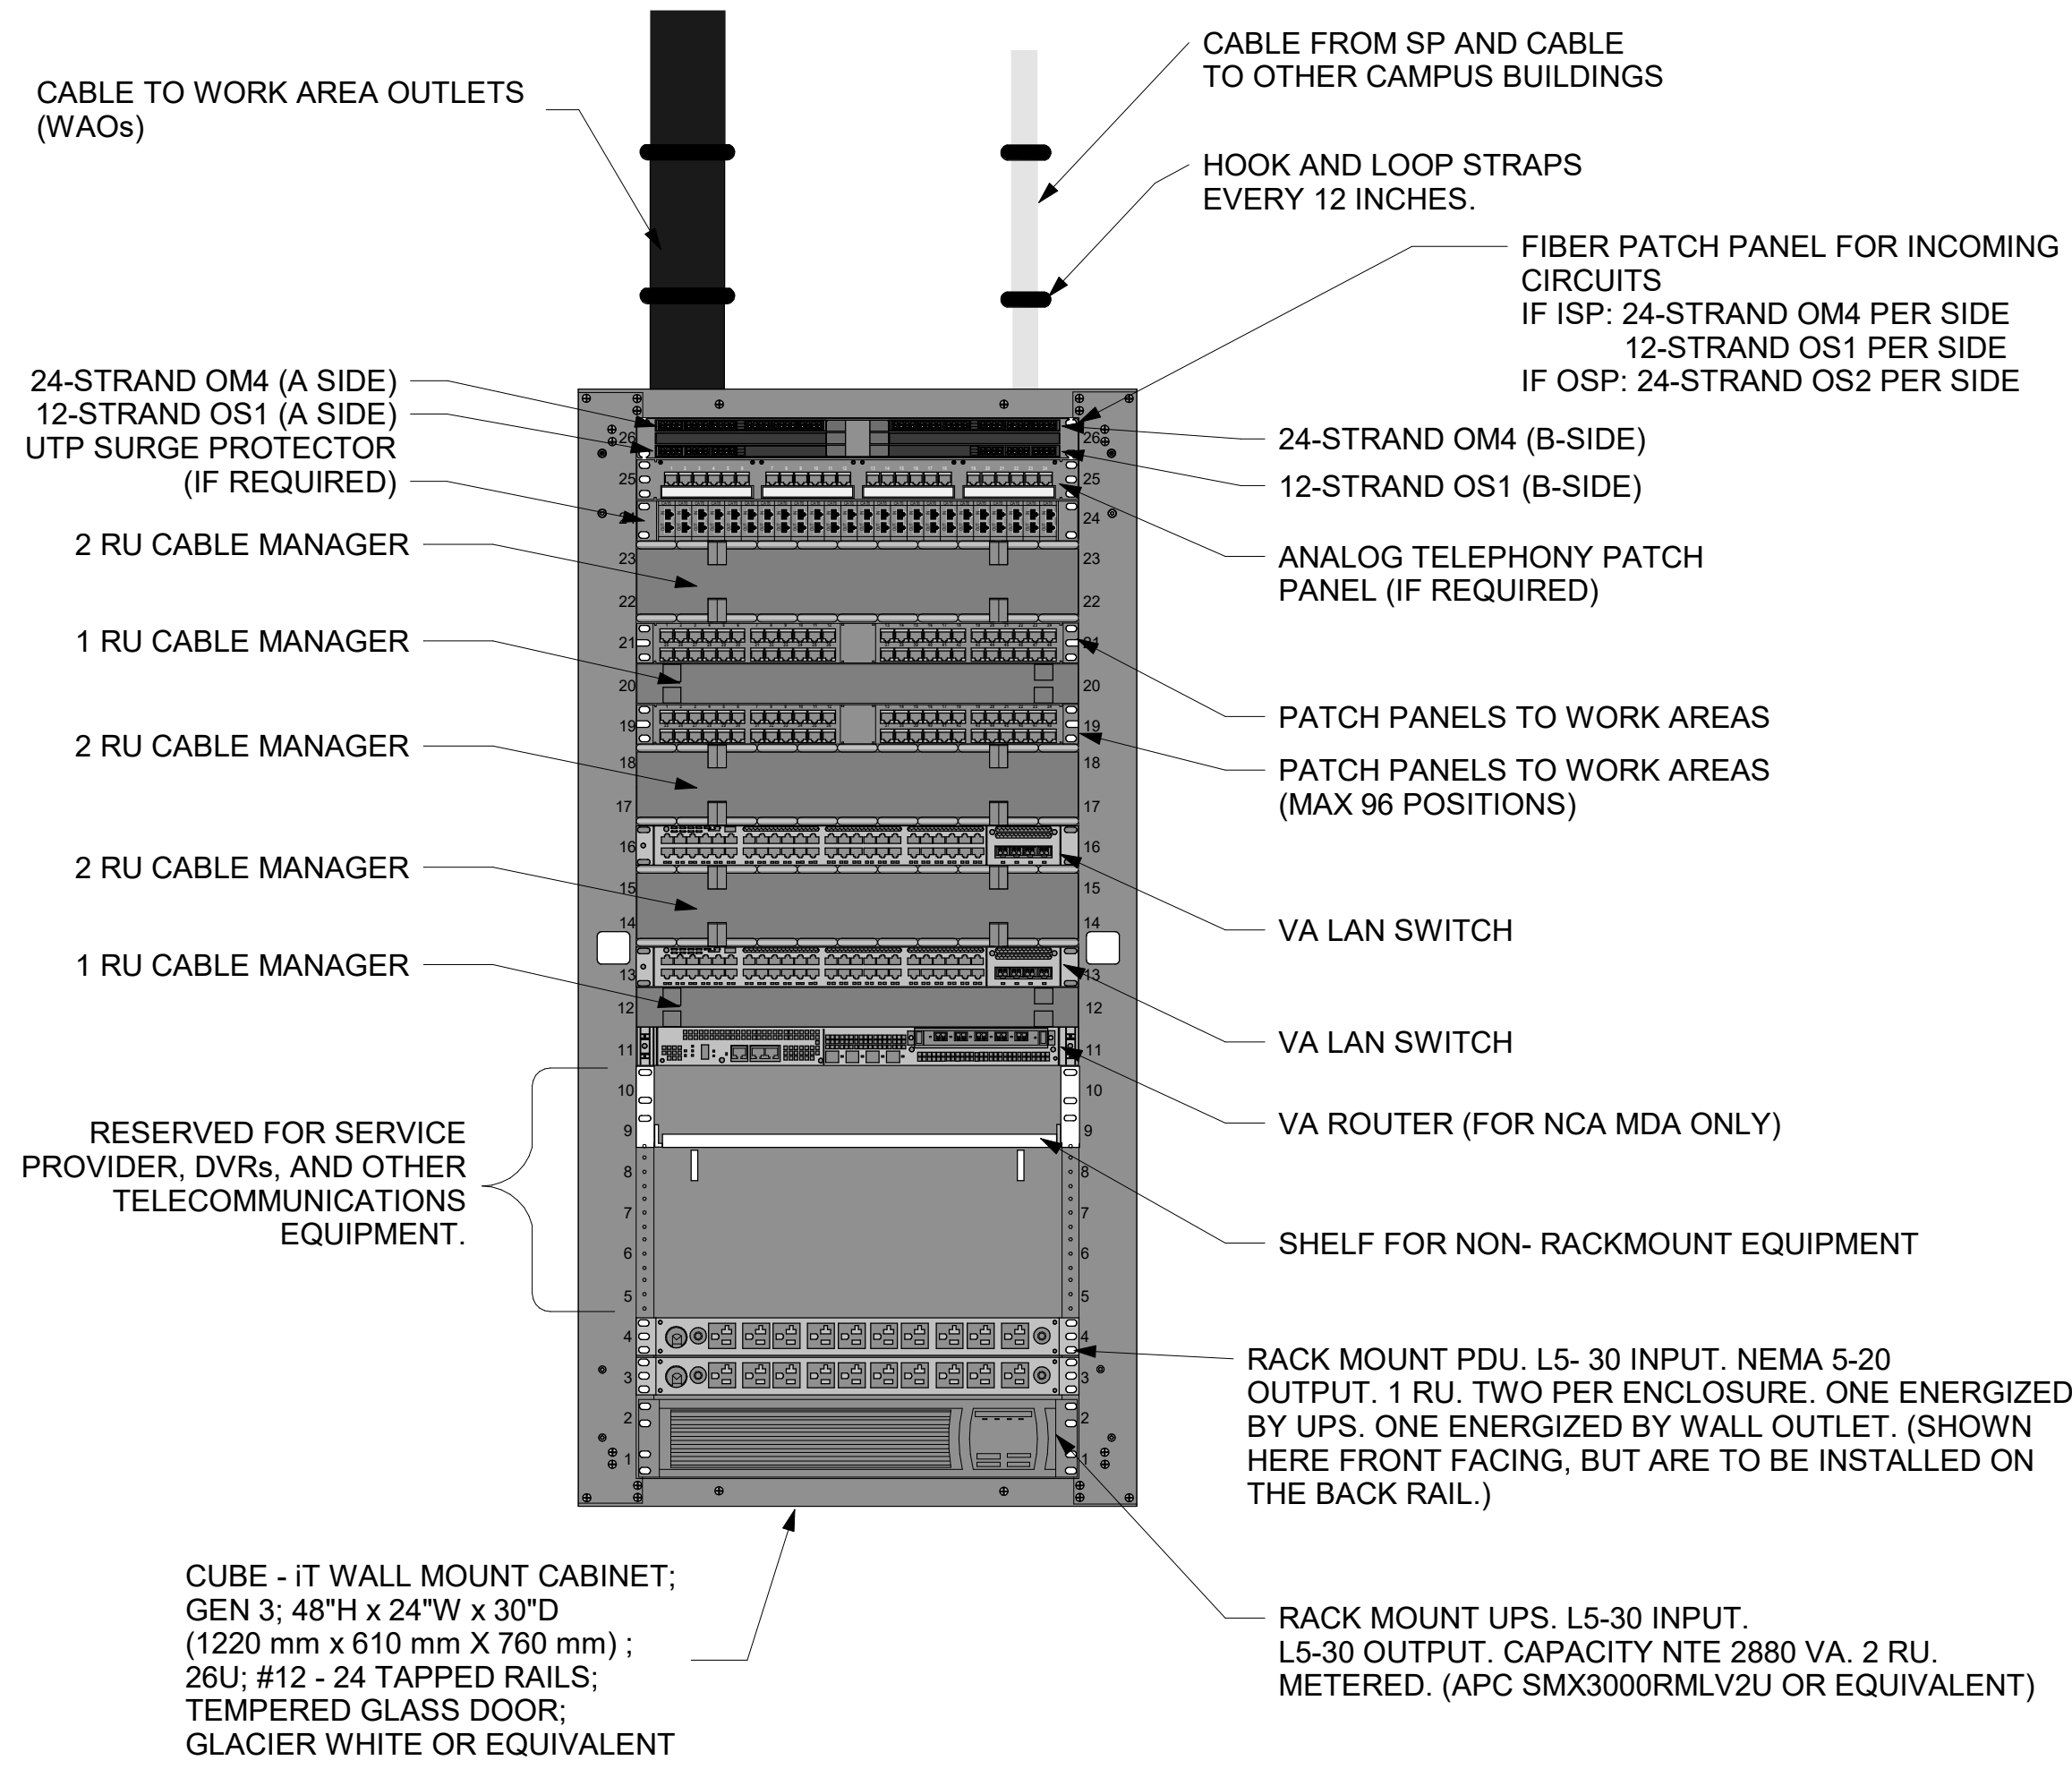


2 TELECOMMUNICATIONS ENCLOSURE ELEVATION DETAIL
NTS

DETAIL IS GENERIC IN NATURE AND SHOWS GENERAL LAYOUT INFORMATION.
REFERENCE GENERAL AND KEY NOTES FOR SPECIFIC INFORMATION

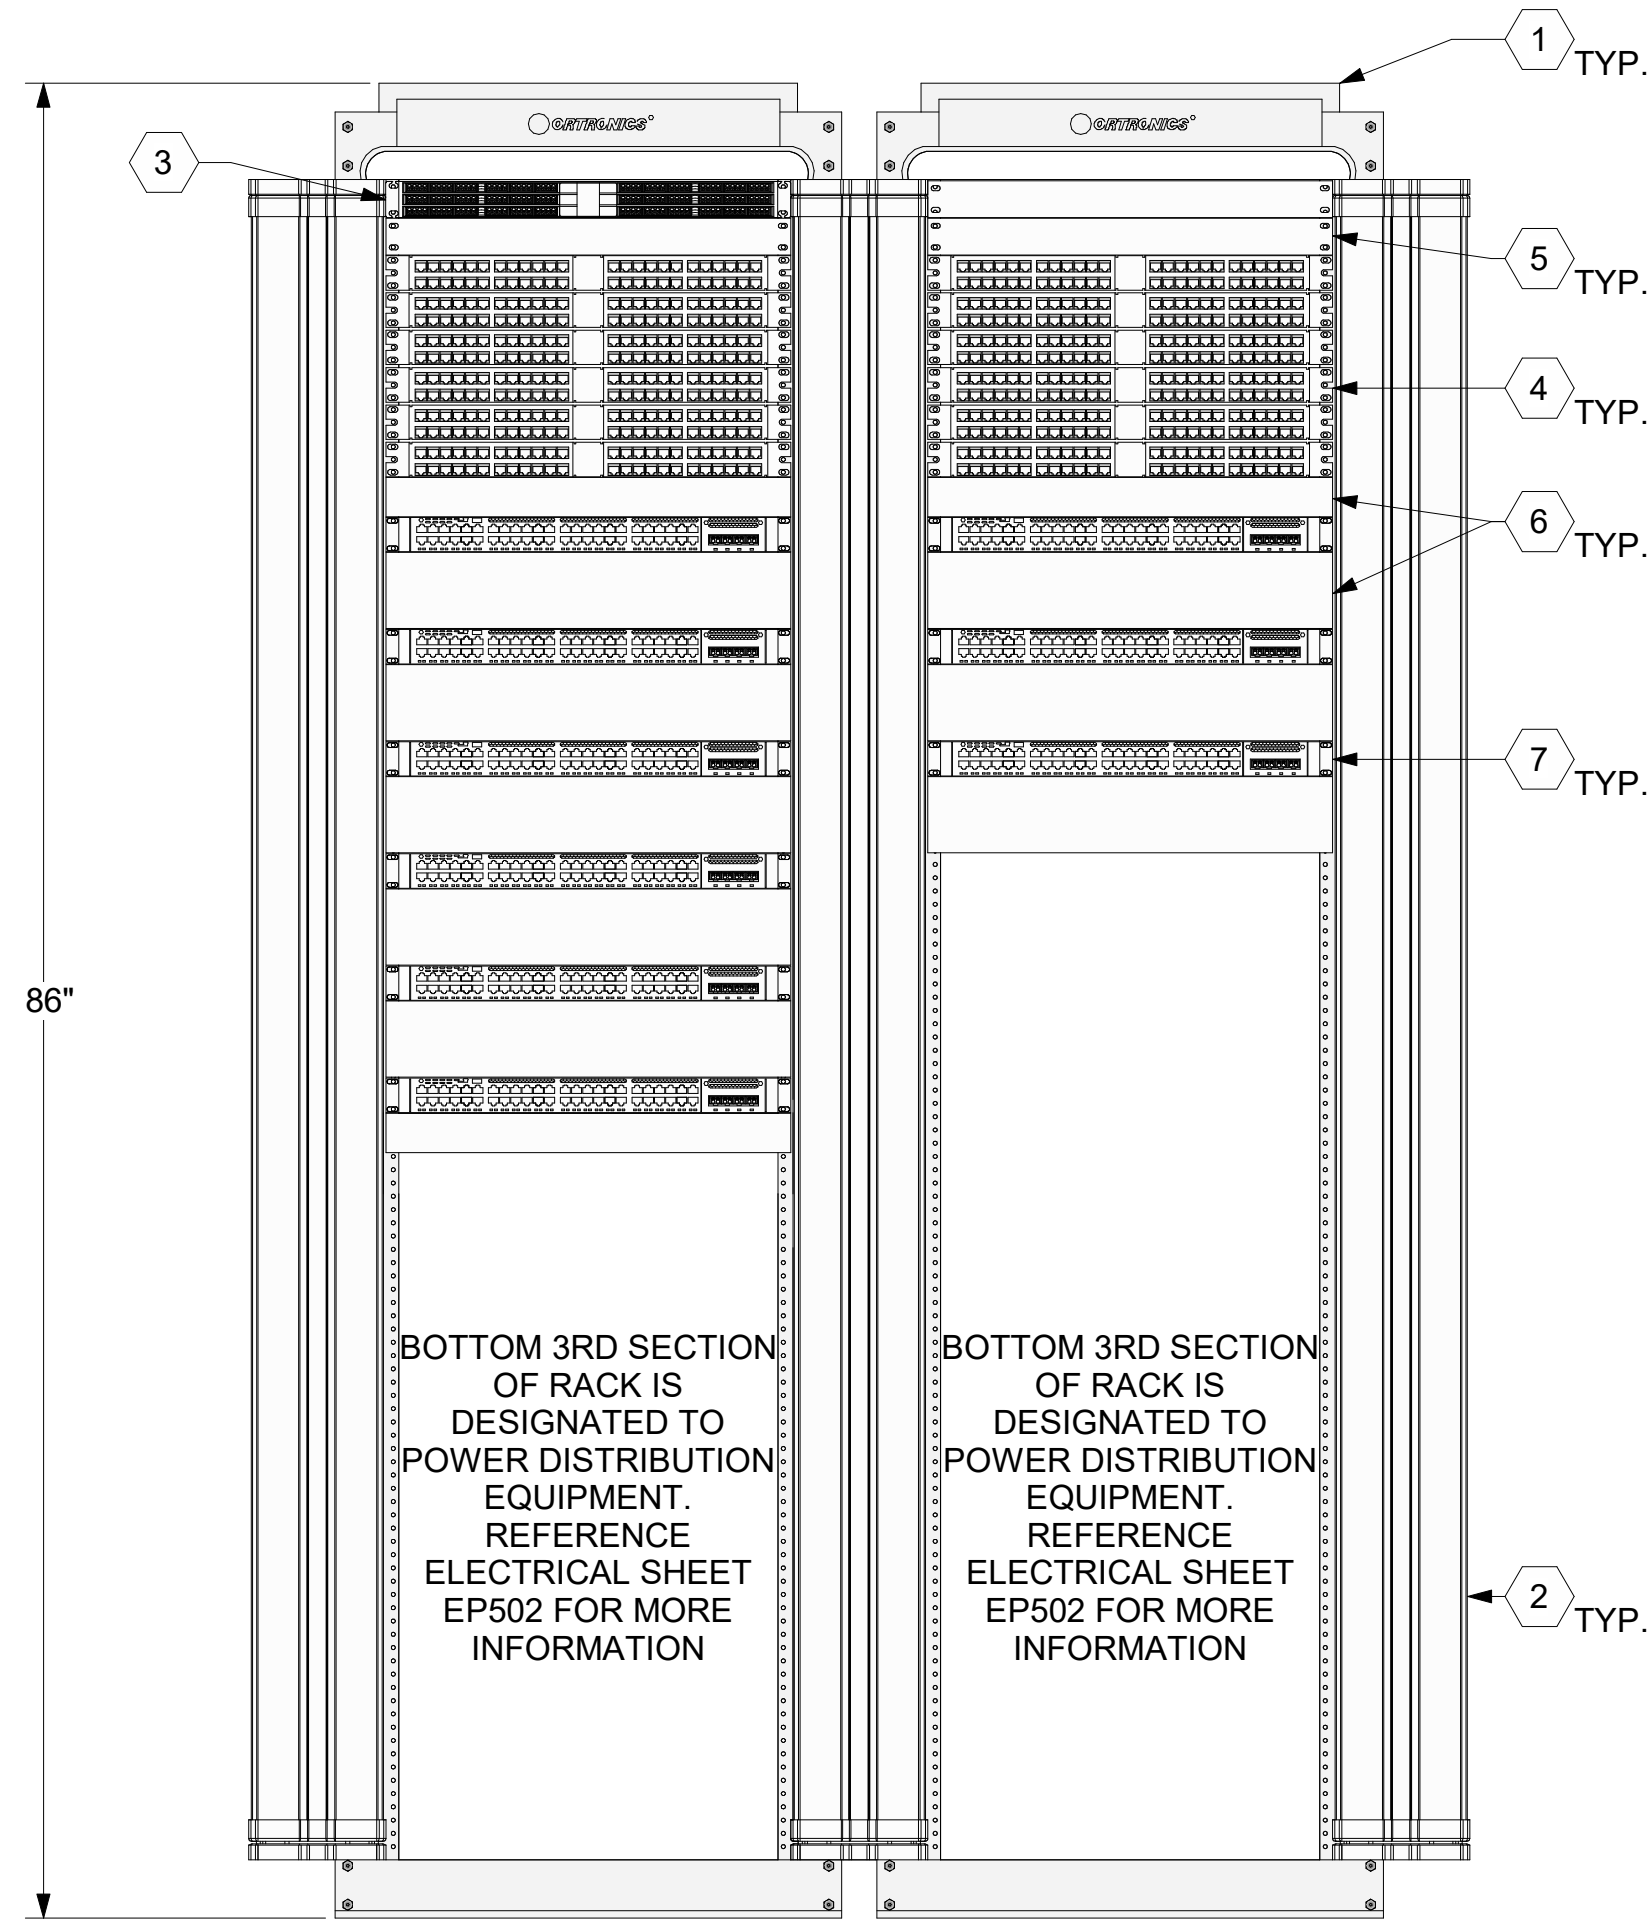

3 TR DATA RACK ELEVATION - TWO RACK
1" = 0'-9"

DETAIL IS GENERIC IN NATURE AND SHOWS GENERAL LAYOUT INFORMATION.
REFERENCE GENERAL AND KEY NOTES FOR SPECIFIC INFORMATION

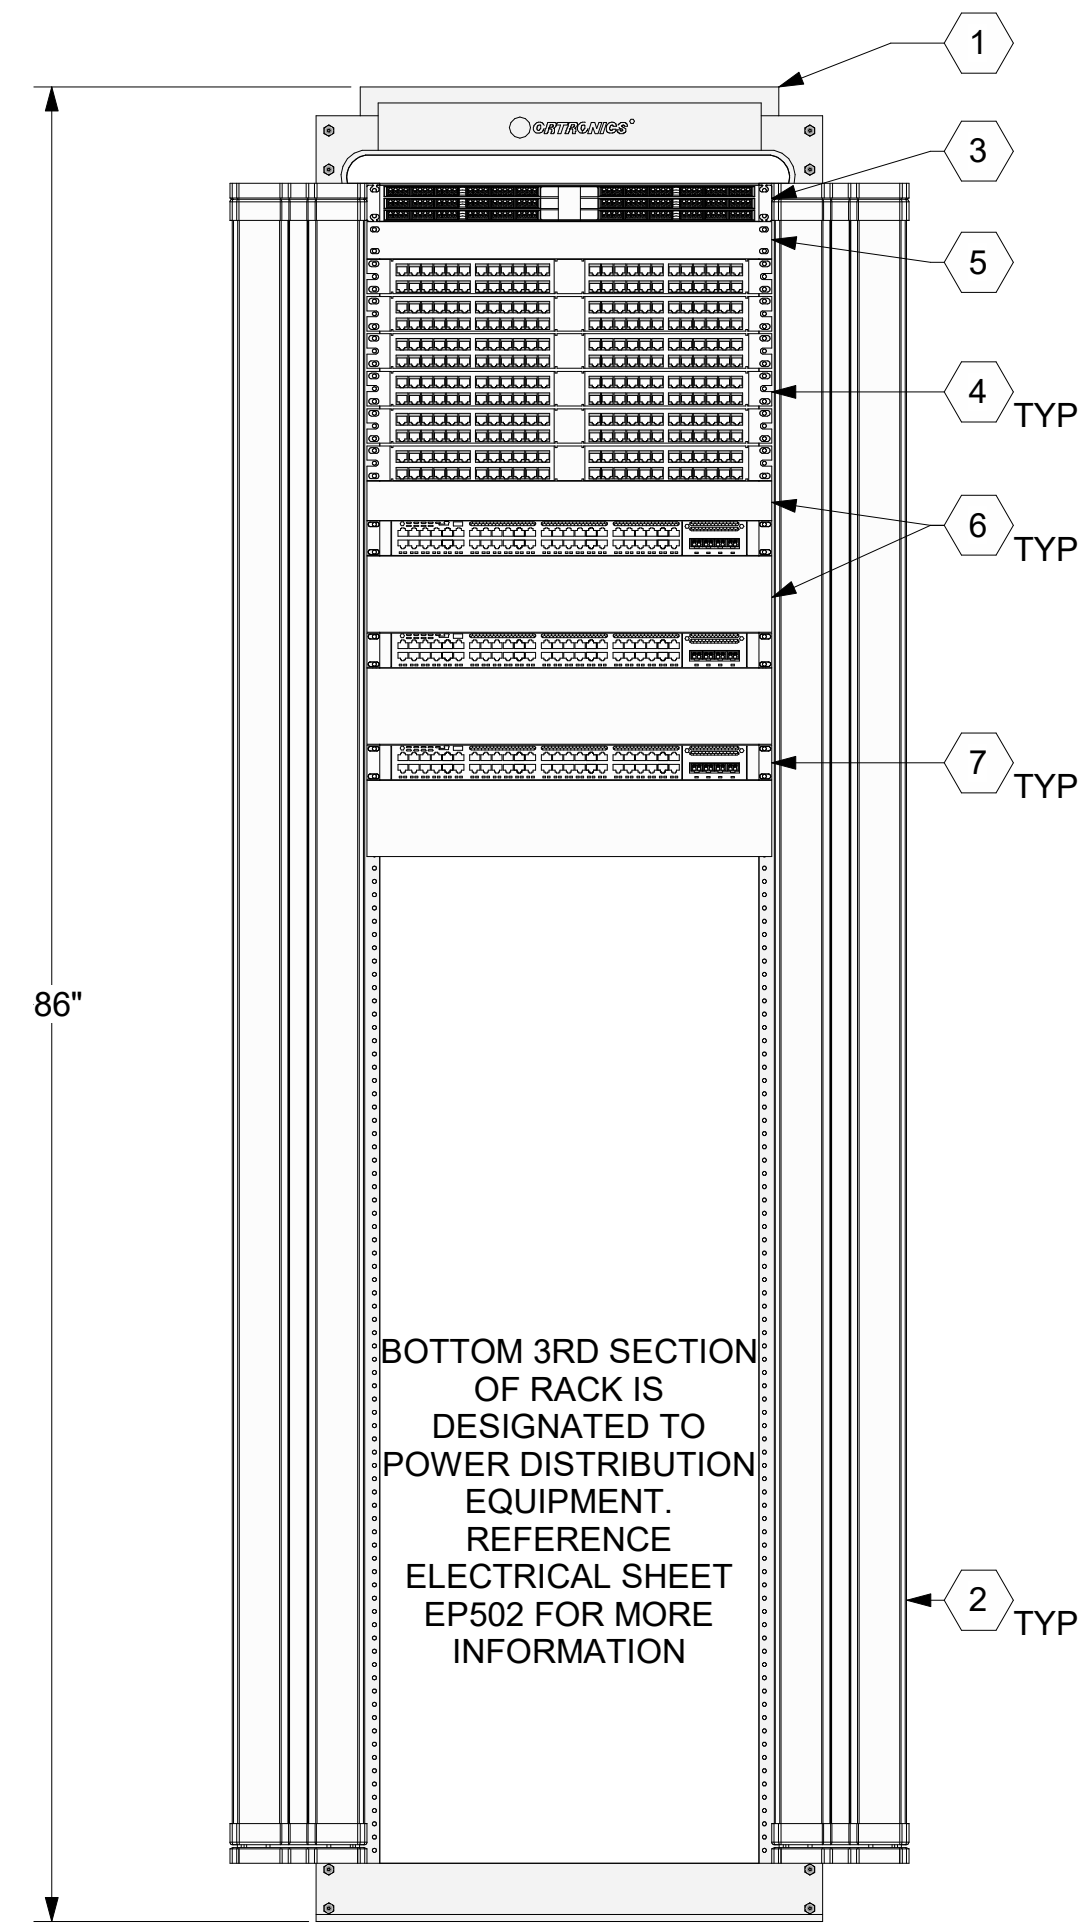

4 TR DATA RACK ELEVATION - SINGLE RACK
1" = 0'-9"

KEY NOTES (FOR THIS SHEET ONLY)

- DATA RACK, 4-POST, WHITE FINISH, ORTRONICS #MM2073038-W, OR APPROVED EQUAL.
- VERTICAL CABLE MANAGER WITH DOOR, 6" WIDE, ORTRONICS #MM20VMD706, OR APPROVED EQUAL.
- FIBER DISTRIBUTION CABINET, ANGLED, 1RU, LEVITON ANGLED OPT-X UHDX, OR APPROVED EQUAL. CABINET POPULATED WITH (12) CASSETTES, LEVITON HDX ENTERPRISE MTP, OR APPROVED EQUAL. SIDE-A AND SIDE-B FIBER BACKBONE SHALL TERMINATE TO SEPARATE SIDES OF DISTRIBUTION CABINET.
- CAT 6A UTP PATCH PANEL, ANGLED, 48-PORT WITH REAR CABLE MANAGER, LEVITON #E2XHD-BLK, OR APPROVED EQUAL.
- BLANKING PANEL, 1RU, LEVITON, OR APPROVED EQUAL.
- HORIZONTAL CABLE MANAGER, 1RU OR 2RU AS SHOWN, LEVITON, OR APPROVED EQUAL.
- NETWORK SWITCH, VA PROVIDED, VA INSTALLED. COORDINATE WITH VA FOR EXACT REQUIREMENTS AS NECESSARY.

CONSULTANT

ENGINEERING DISCIPLINE:

ARCHITECT/ENGINEER OF RECORD

A/E:
SPEES DESIGN BUILD
23830 PACIFIC HIGHWAY S. SUITE 203
KENT, WA 98032



STAMP



Office of
Construction
and Facilities
Management



U.S. Department
of Veterans Affairs

Drawing Title

TELECOMMUNICATIONS DETAILS

Approved:

Phase

100% CONSTRUCTION
DOCUMENTS

FULLY SPRINKLERED

Project Title

EHRM INFRASTRUCTURE
UPGRADES - HAMPTON

Location

HAMPTON VA MEDICAL CENTER, HAMPTON, VIRGINIA

Issue Date

07/18/2025

Checked

KG

Drawn

BCL/GPB

Project Number

590-22-700

Building Number

-

Drawing Number


TN502

619 of 713


A

B

C

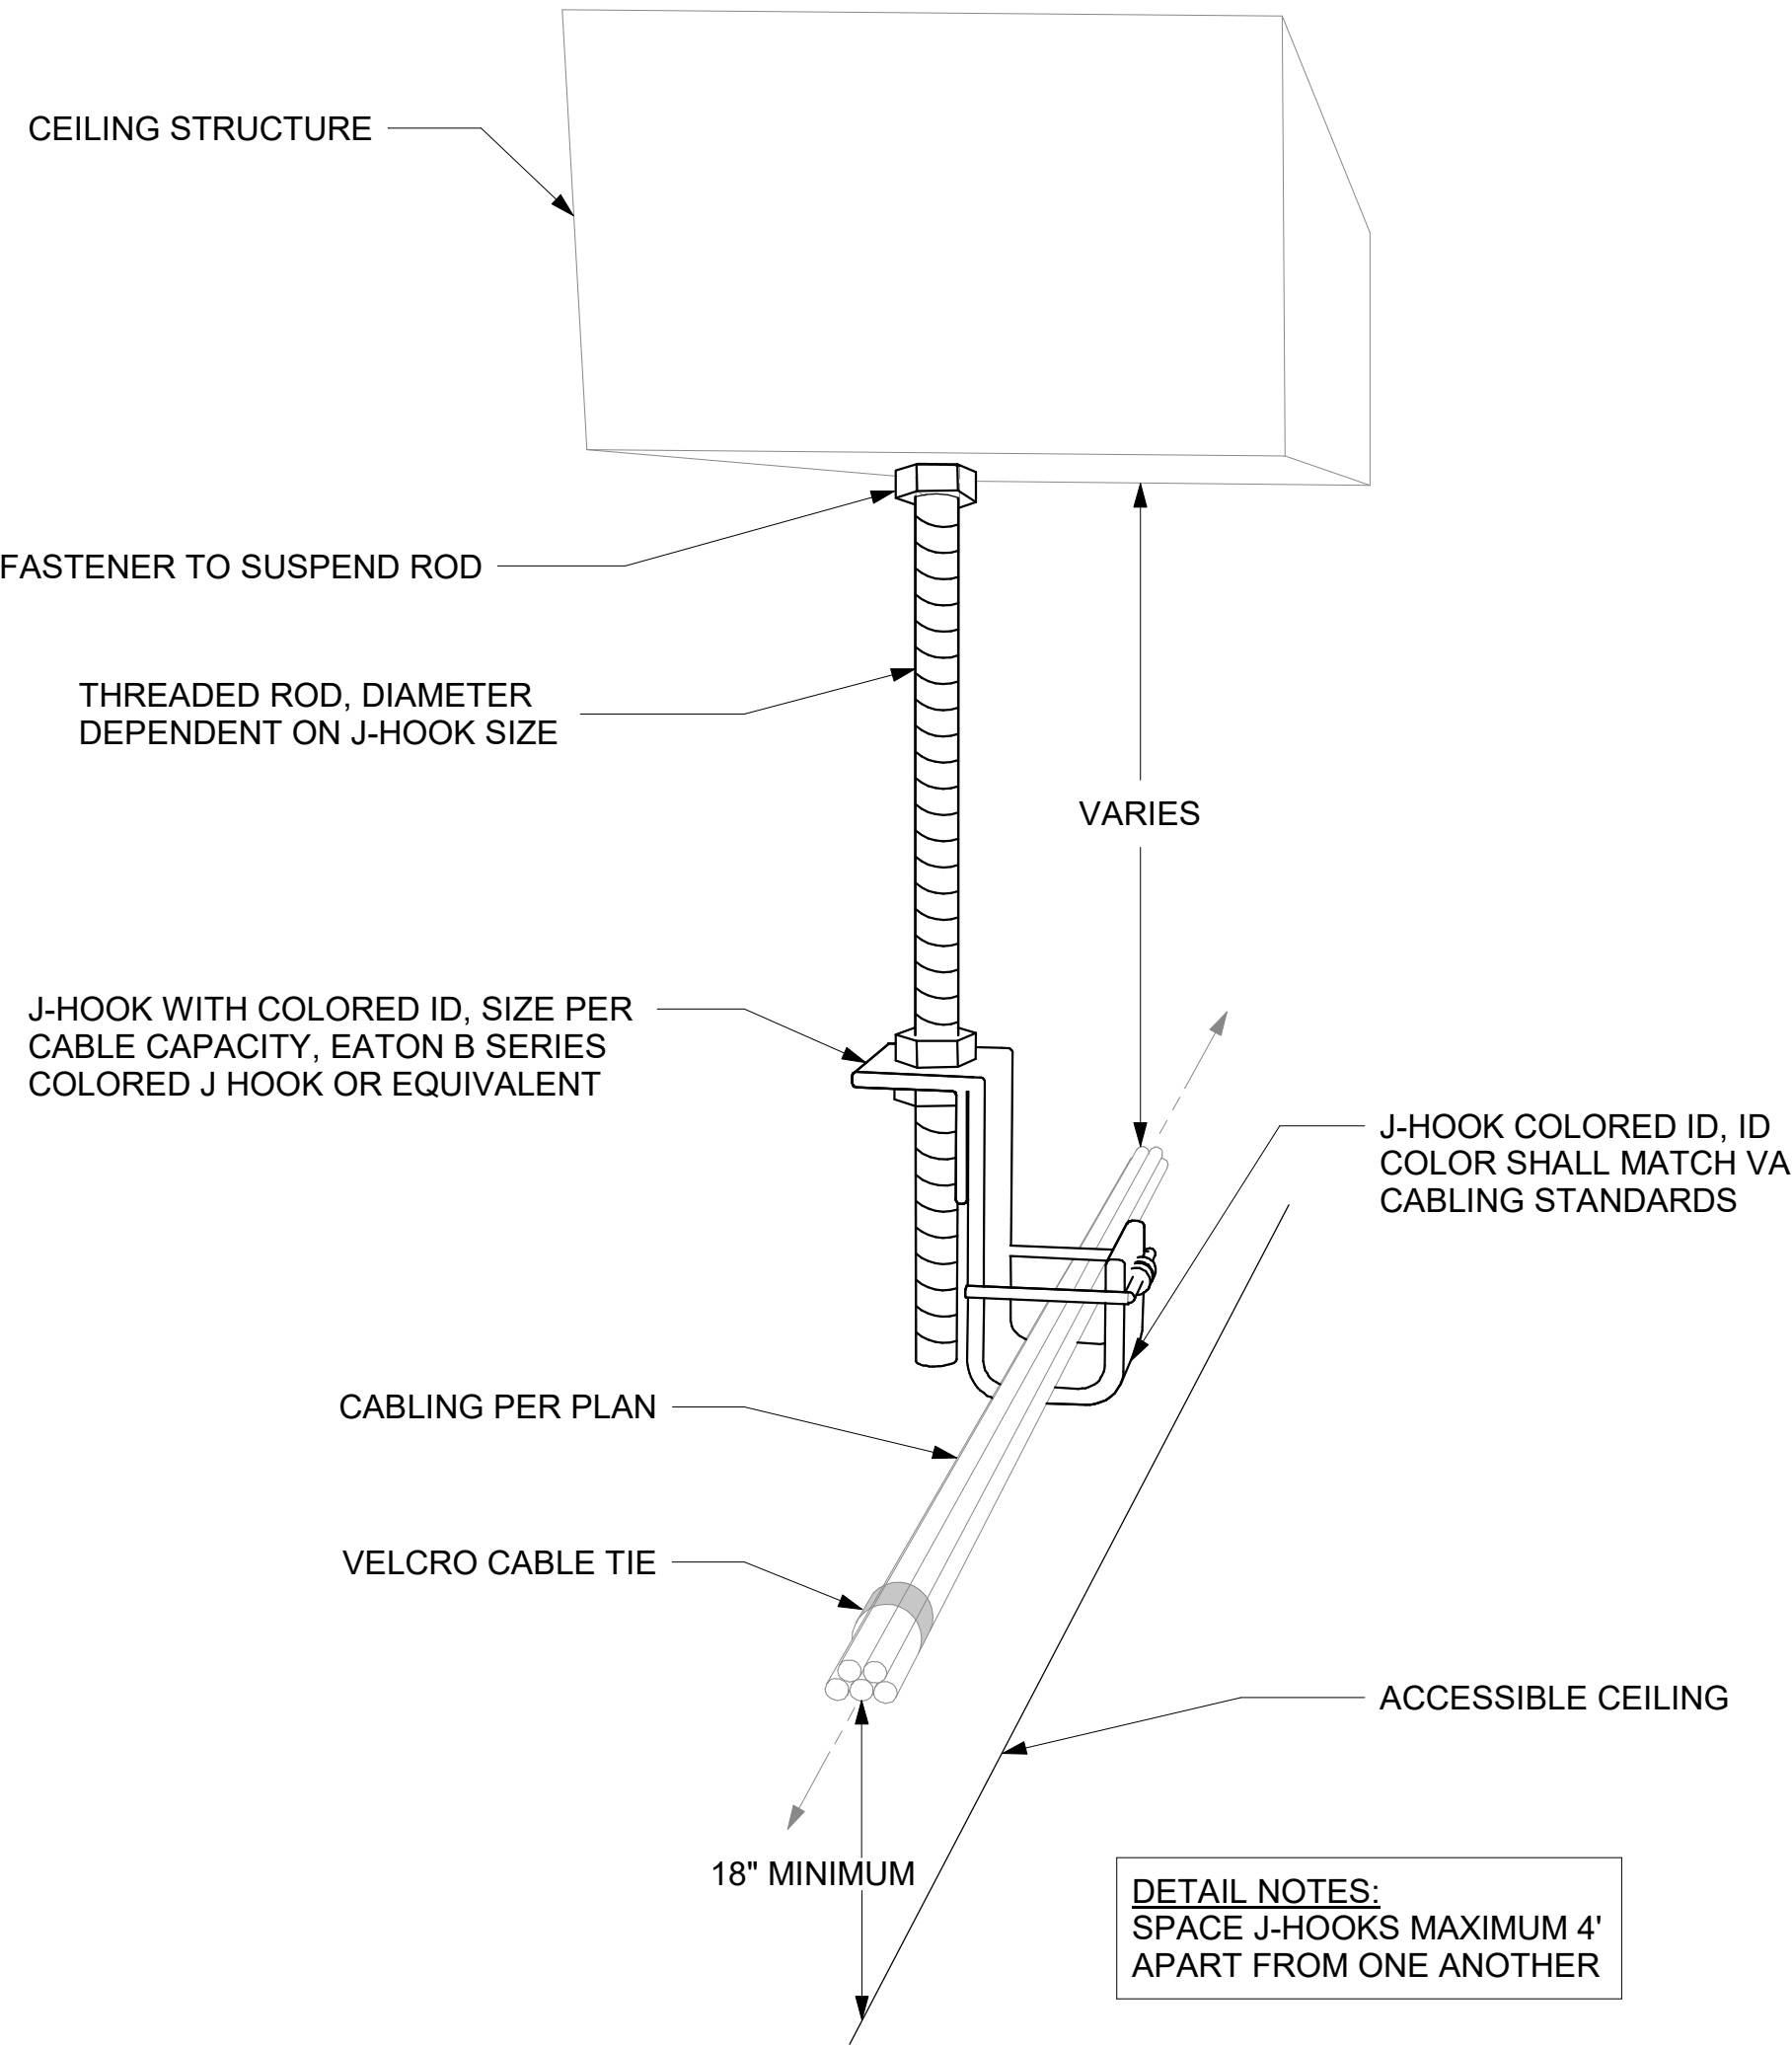

1 TYPICAL J-HOOK INSTALLATION DETAIL
NTS

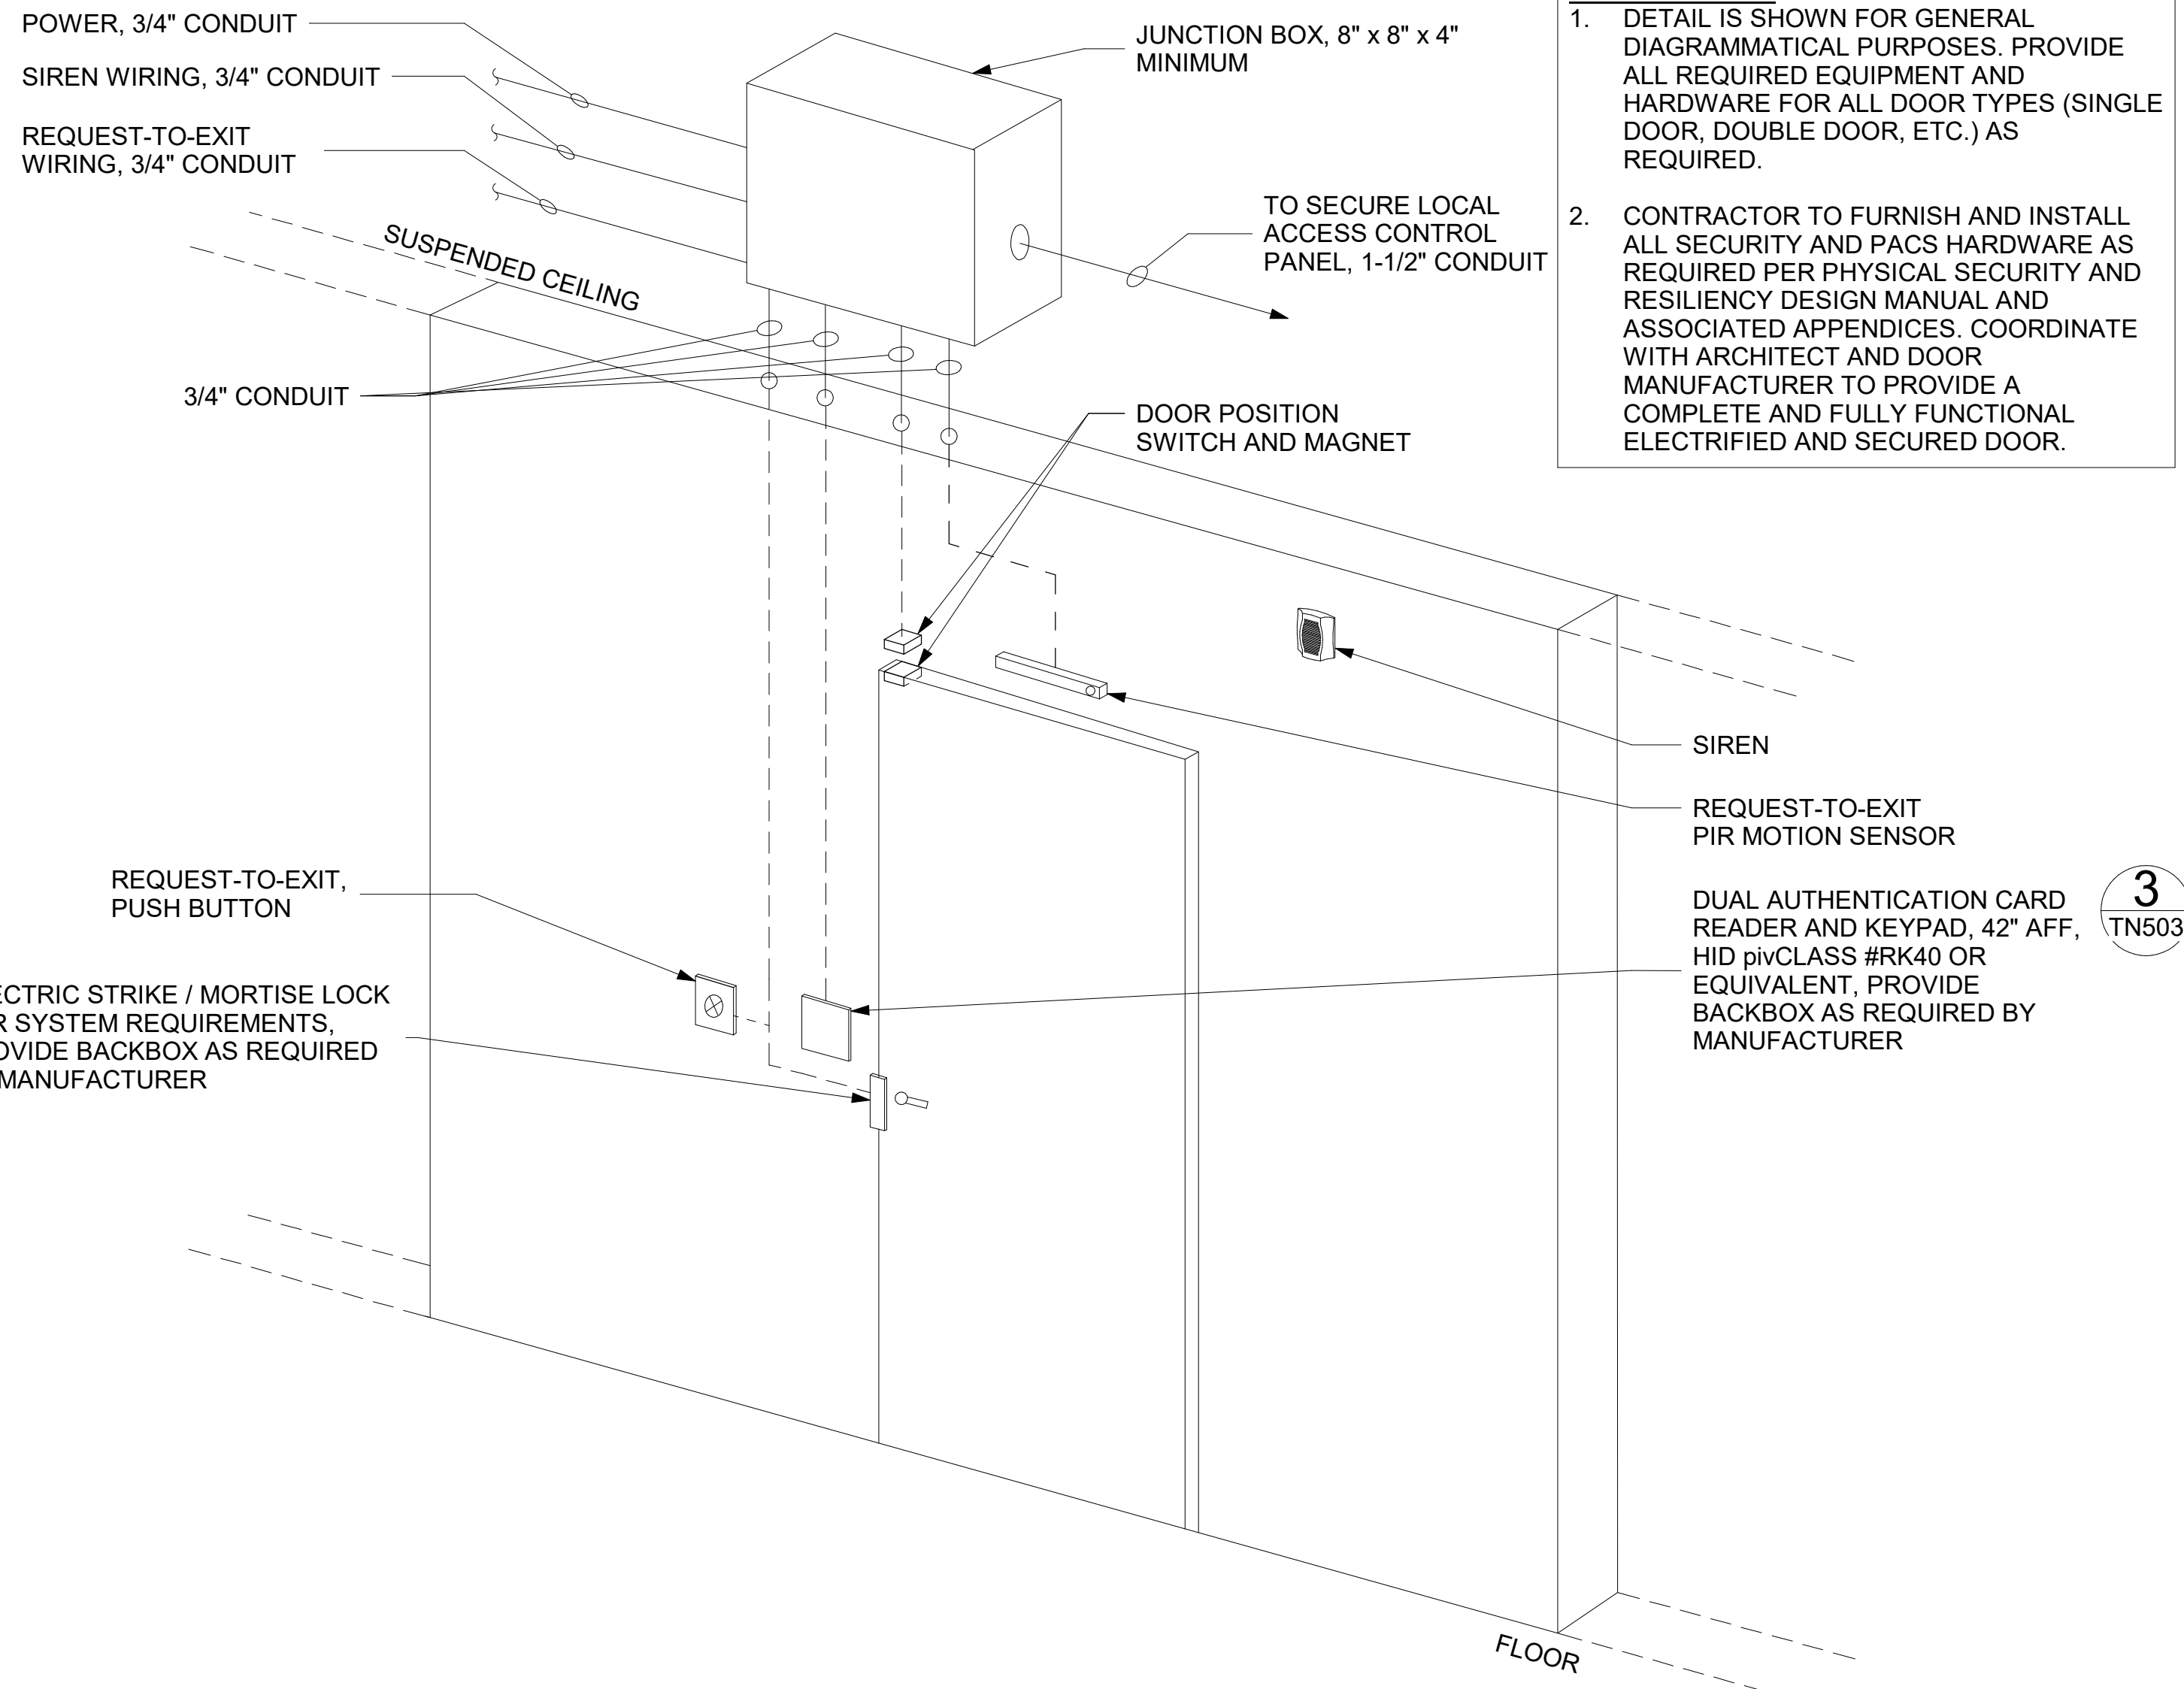

2 SECURITY DOOR CARD READER INSTALLATION DETAIL
NTS

GENERAL NOTES


- DETAILS NOTES:
1. DETAIL IS SHOWN FOR GENERAL DIAGRAMMATICAL PURPOSES. PROVIDE ALL REQUIRED EQUIPMENT AND HARDWARE FOR ALL DOOR TYPES (SINGLE DOOR, DOUBLE DOOR, ETC.) AS REQUIRED.
 2. CONTRACTOR TO FURNISH AND INSTALL ALL SECURITY AND PACS HARDWARE AS REQUIRED PER PHYSICAL SECURITY AND RESILIENCY DESIGN MANUAL AND ASSOCIATED APPENDICES. COORDINATE WITH ARCHITECT AND DOOR MANUFACTURER TO PROVIDE A COMPLETE AND FULLY FUNCTIONAL ELECTRIFIED AND SECURED DOOR.

3
TN503

D




E

F

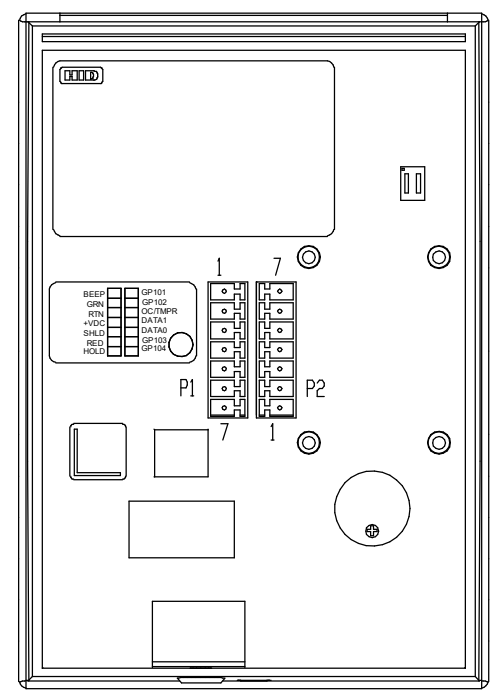


PIV ENABLED TWO-FACTOR AUTHENTICATION KEY PAD AND CONTACTLESS AUTHENTICATION, HID pivCLASS #RK40 OR EQUIVALENT

WIRING TABLE		
PIGTAIL- WIRE COLOR	TERM STRIP - CONNECTION	CIRCUIT FUNCTION
YELLOW	P1-1	NO CONNECT
ORANGE	P1-2	NO CONNECT
BLACK	P1-3	RTN
RED	P1-4	+VDC
DRAIN	P1-5	NO CONNECT
BROWN	P1-6	NO CONNECT
BLUE	P1-7	NO CONNECT
GRAY	P2-1	RS485 / TXA
PINK	P2-2	RS485 / TXB
GREEN	P2-3	NO CONNECT
WHITE	P2-4	NO CONNECT
VIOLET	P2-5	NO CONNECT
TAN	P2-6	RS485 / RXB
RED/GREEN	P2-7	RS485 / RXA

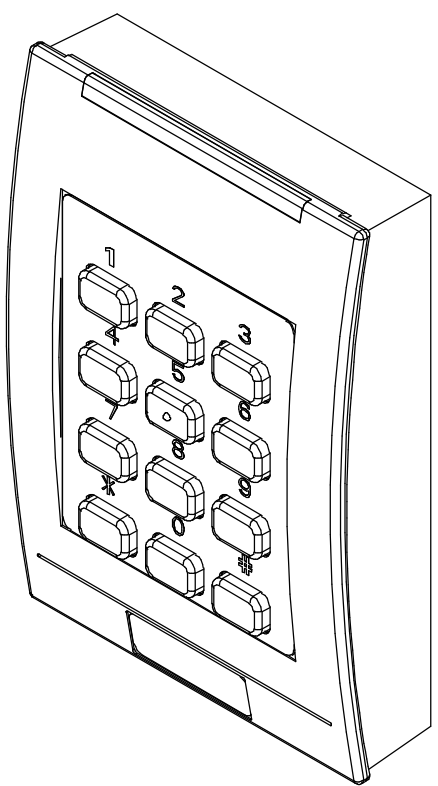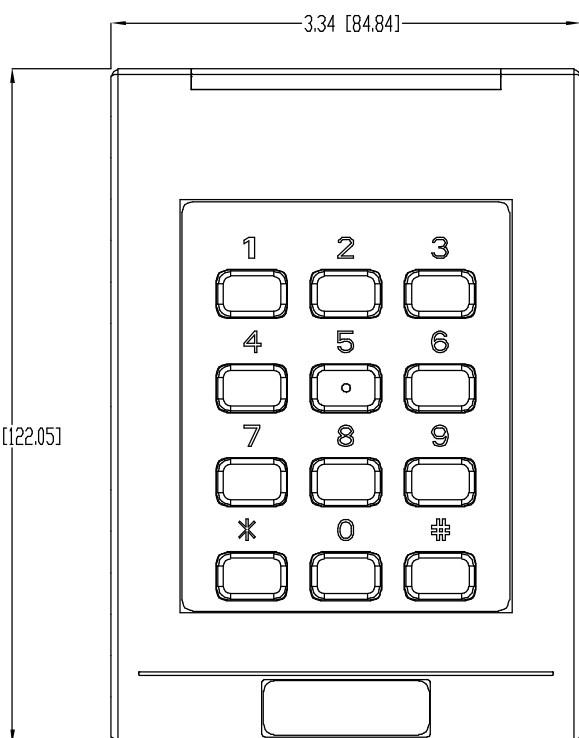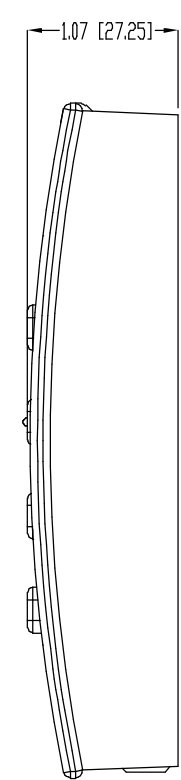


3 TYPICAL CONTACTLESS AUTHENTICATION AND PINPAD DEVICE
NTS

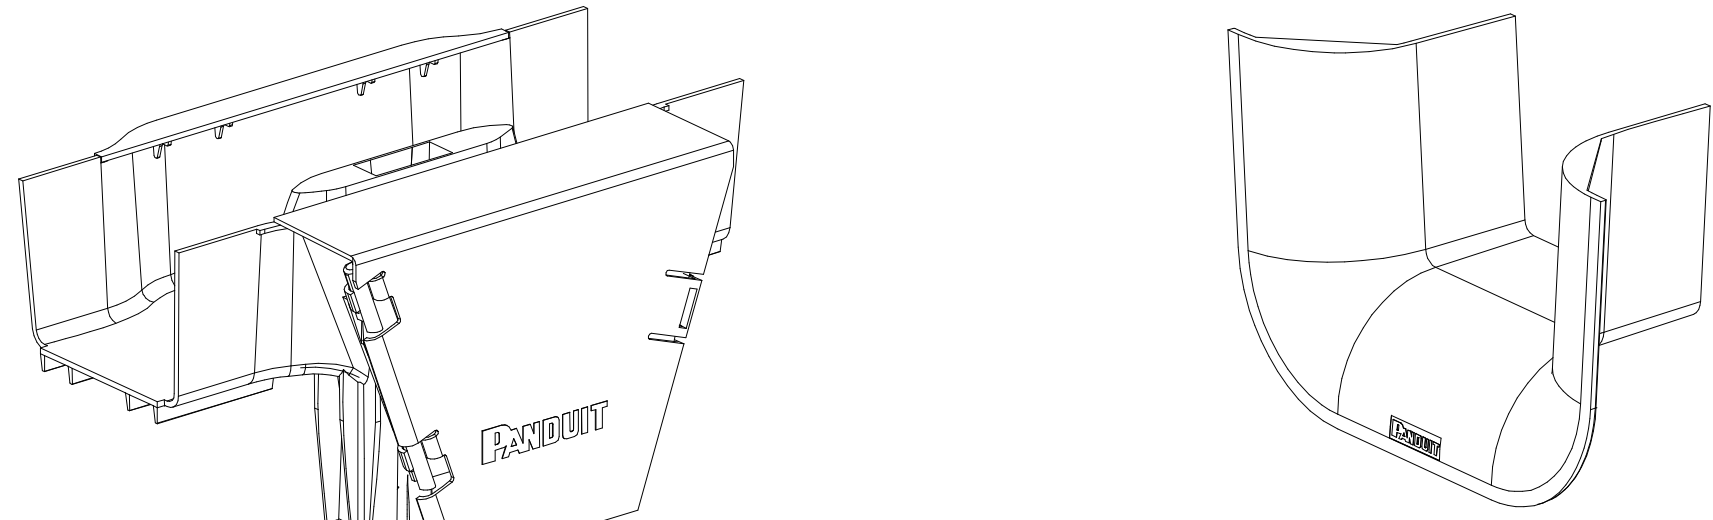


FIBER PATHWAY BEND RADIUS SPILLWAYS (PANDUIT FRVT4X4/FRTR4X4 OR EQUIVALENT):

VERTICAL TEE
TRUMPET SPILLWAY
BEND RADIUS SPILLWAYS REQUIRED AT EVERY RACK LOCATION

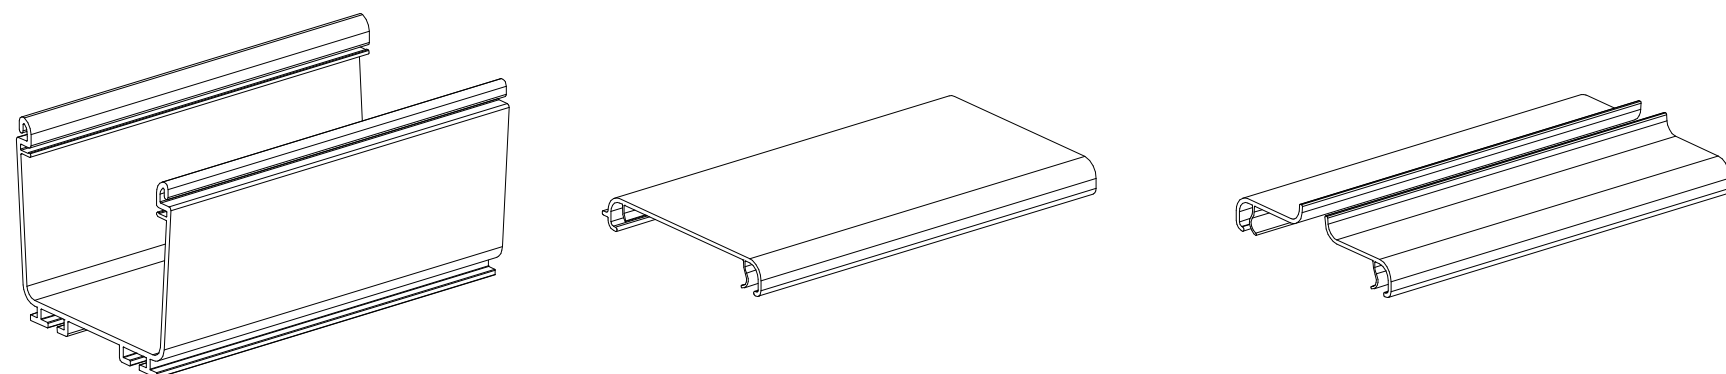

FIBER PATHWAY CHANNEL AND COVERS (PANDUIT FR4X4/FRHC4/FRSHC4 OR EQUIVALENT):

4X4" CHANNEL COVER
SOLID COVER
SPLIT HINGED COVER

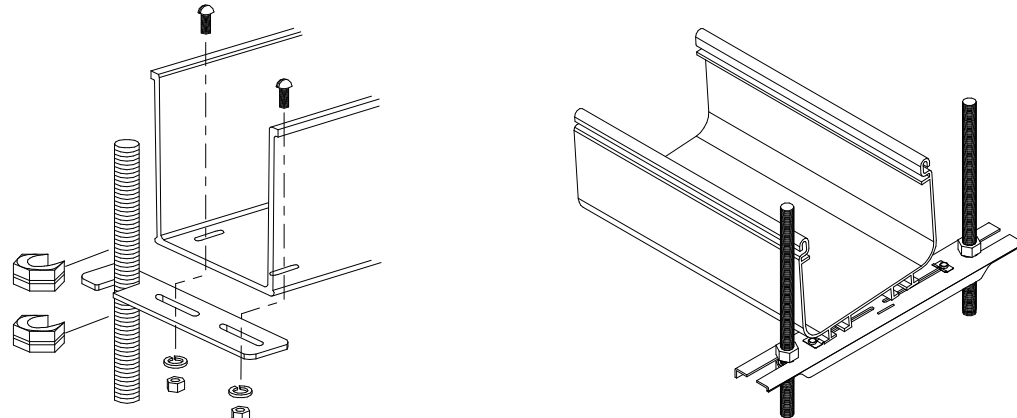

FIBER PATHWAY MOUNTING BRACKET (PANDUIT FR6TRBE/FR6TBN OR EQUIVALENT):

BRACKET TO MOUNT TO EXISTING THREADED ROD OR
BRACKET TO MOUNT TO NEW THREADED ROD

4 FIBER PATHWAY AND DETAILS
NTS

KEY NOTES

GENERAL NOTES


1. THIS SHEET SHALL BE PRINTED IN COLOR TO PROVIDE ALL NECESSARY INFORMATION.

1 NOT USED
NTS

2 NOT USED
NTS

3 NOT USED
NTS

4 TYPICAL TR LADDER RACK ELEVATION
NTS

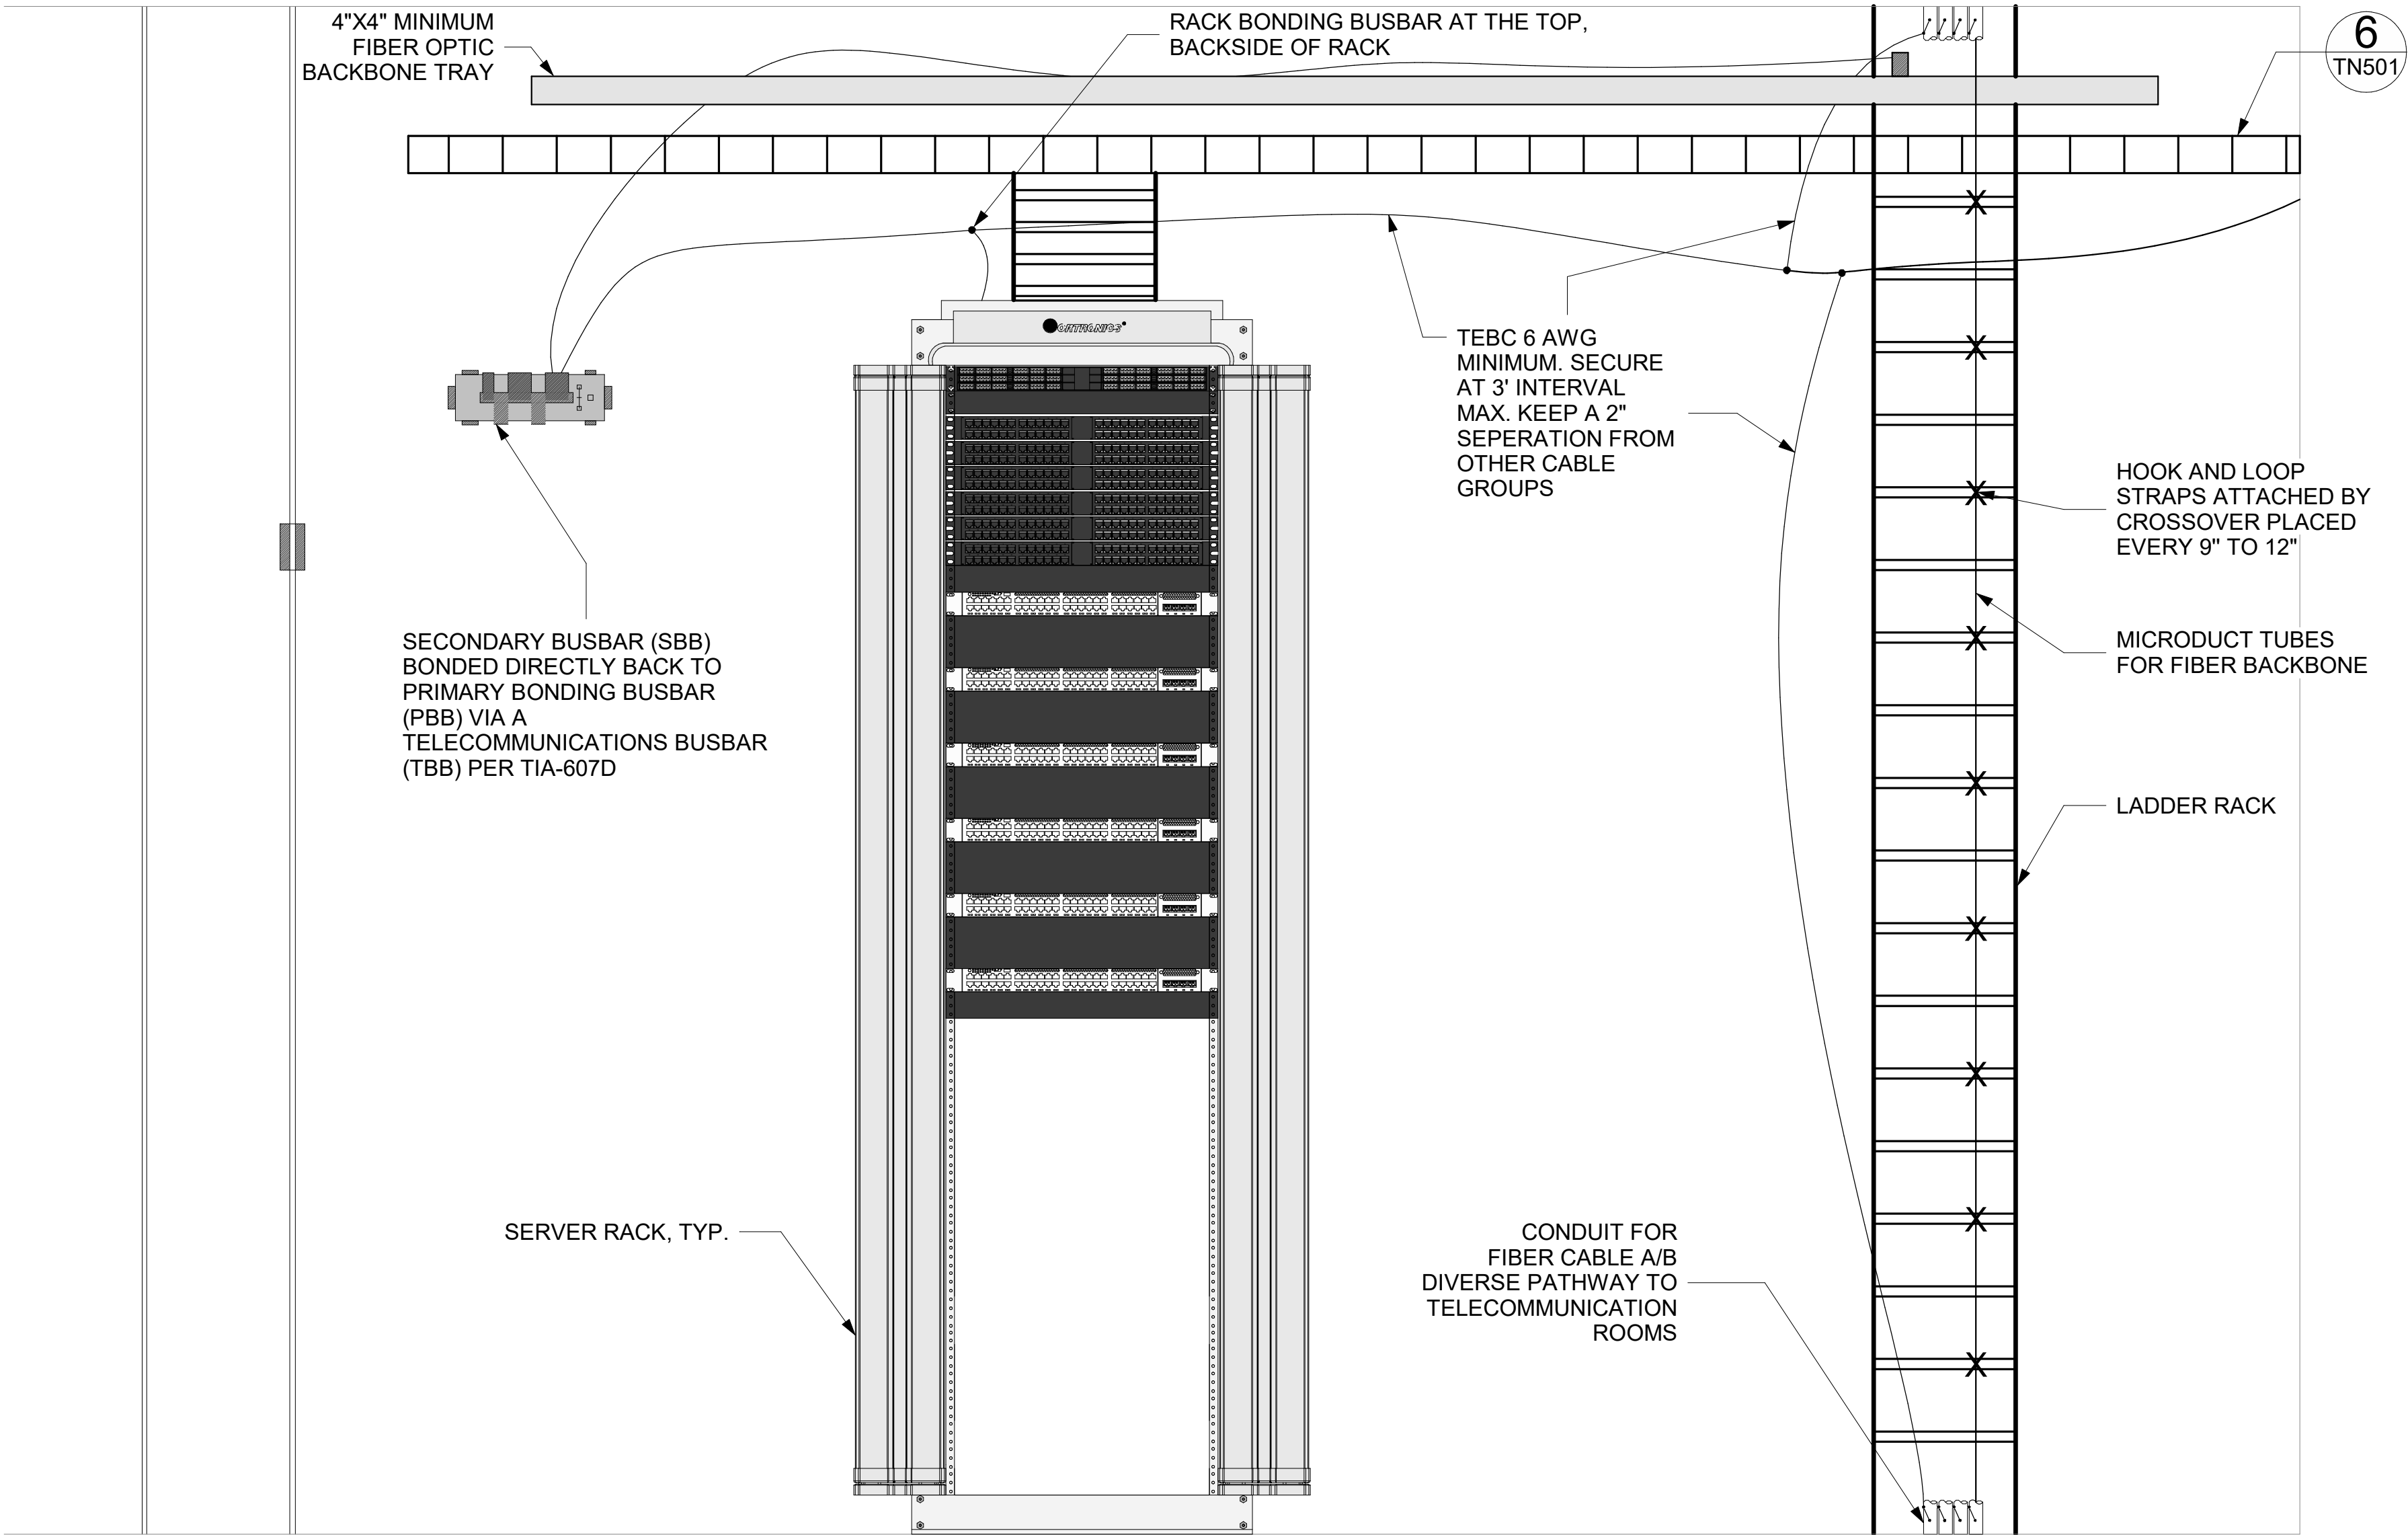

BMA 360/599-22-700
VA Hampton EHRMVA
General Notes, Diagrams and Details.rvt
15/07/2025 8:36:30 am

		CONSULTANT	ARCHITECT/ENGINEER OF RECORD	STAMP	Office of Construction and Facilities Management	Drawing Title	Phase	Project Title	Project Number
		ENGINEERING DISCIPLINE:	A/E:			TELECOMMUNICATIONS DETAILS	100% CONSTRUCTION DOCUMENTS	EHRM INFRASTRUCTURE UPGRADES - HAMPTON	590-22-700
			SPEES DESIGN BUILD						Building Number
			23830 PACIFIC HIGHWAY S. SUITE 203						-
			KENT, WA 98032		VA U.S. Department of Veterans Affairs	Approved:	FULLY SPRINKLERED	Location	Drawing Number
								HAMPTON VA MEDICAL CENTER, HAMPTON, VIRGINIA	TN504
Revisions:	Date:						Issue Date	Checked	Drawn
						07/18/2025	KG	BCL/GPB	

BM 360/599-22-700
VA Hampton EHRMVA
General
Notes, Diagrams and Details.rvt
15/07/2025 8:36:40 am

A

B

C

D

E

F

A

B

C

D

E

F



1 NOT USED
NTS





2 TYPICAL DEVICE MOUNTING HEIGHT DETAIL
NTS

3 CABLE TRAY GROUNDING/BONDING REQUIREMENTS
NTS


4 NOT USED
NTS

DETAIL NOTES(S):
1. THESE TYPICAL MOUNTING HEIGHTS SHALL BE USED UNLESS OTHERWISE NOTED.

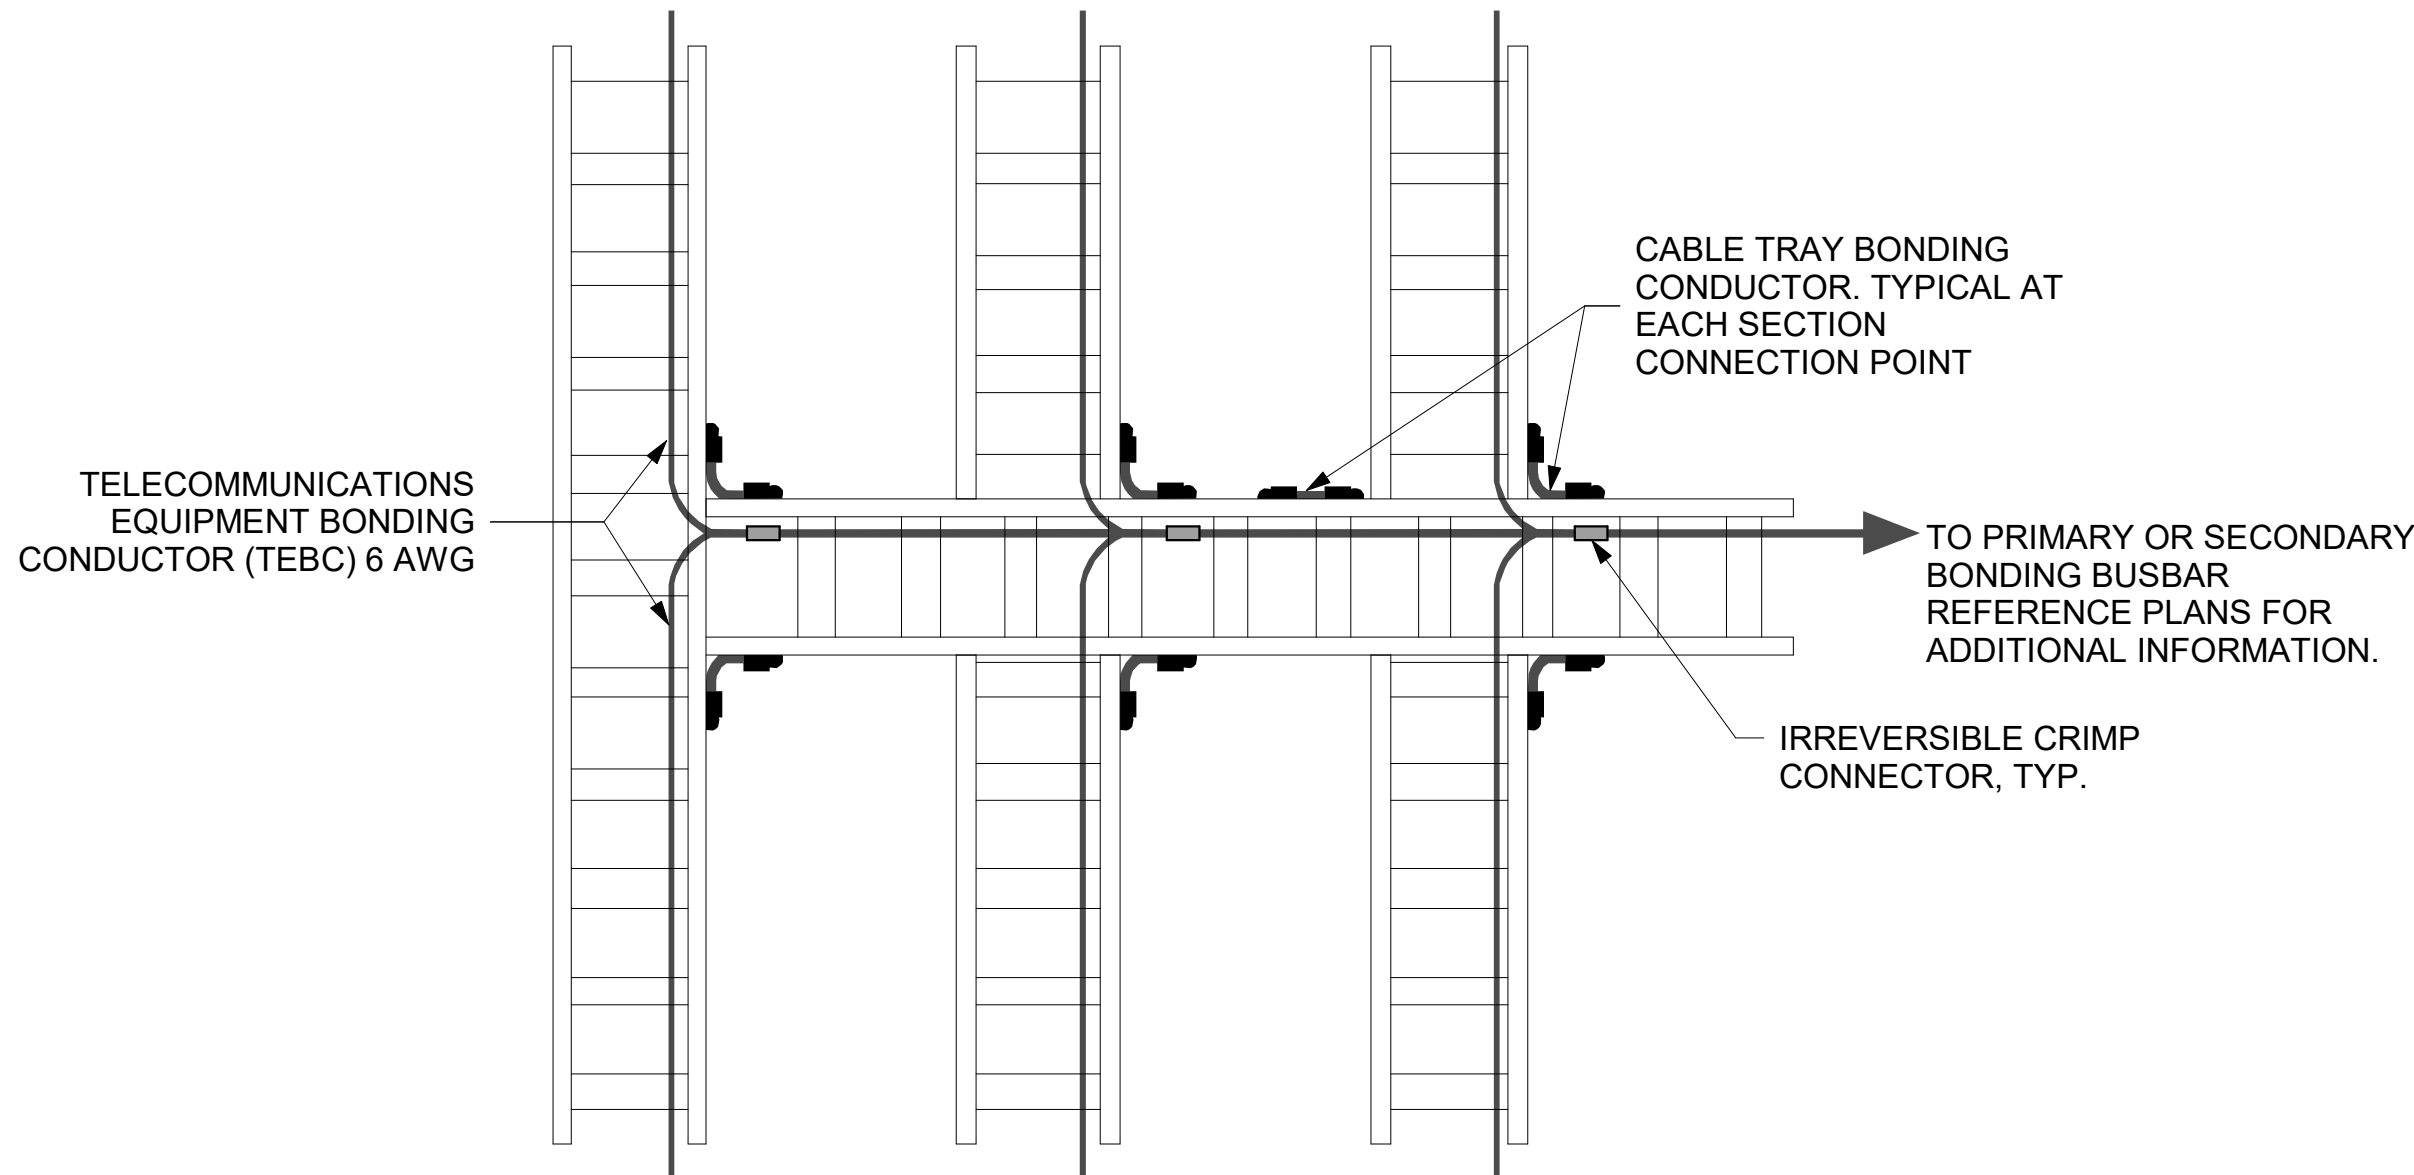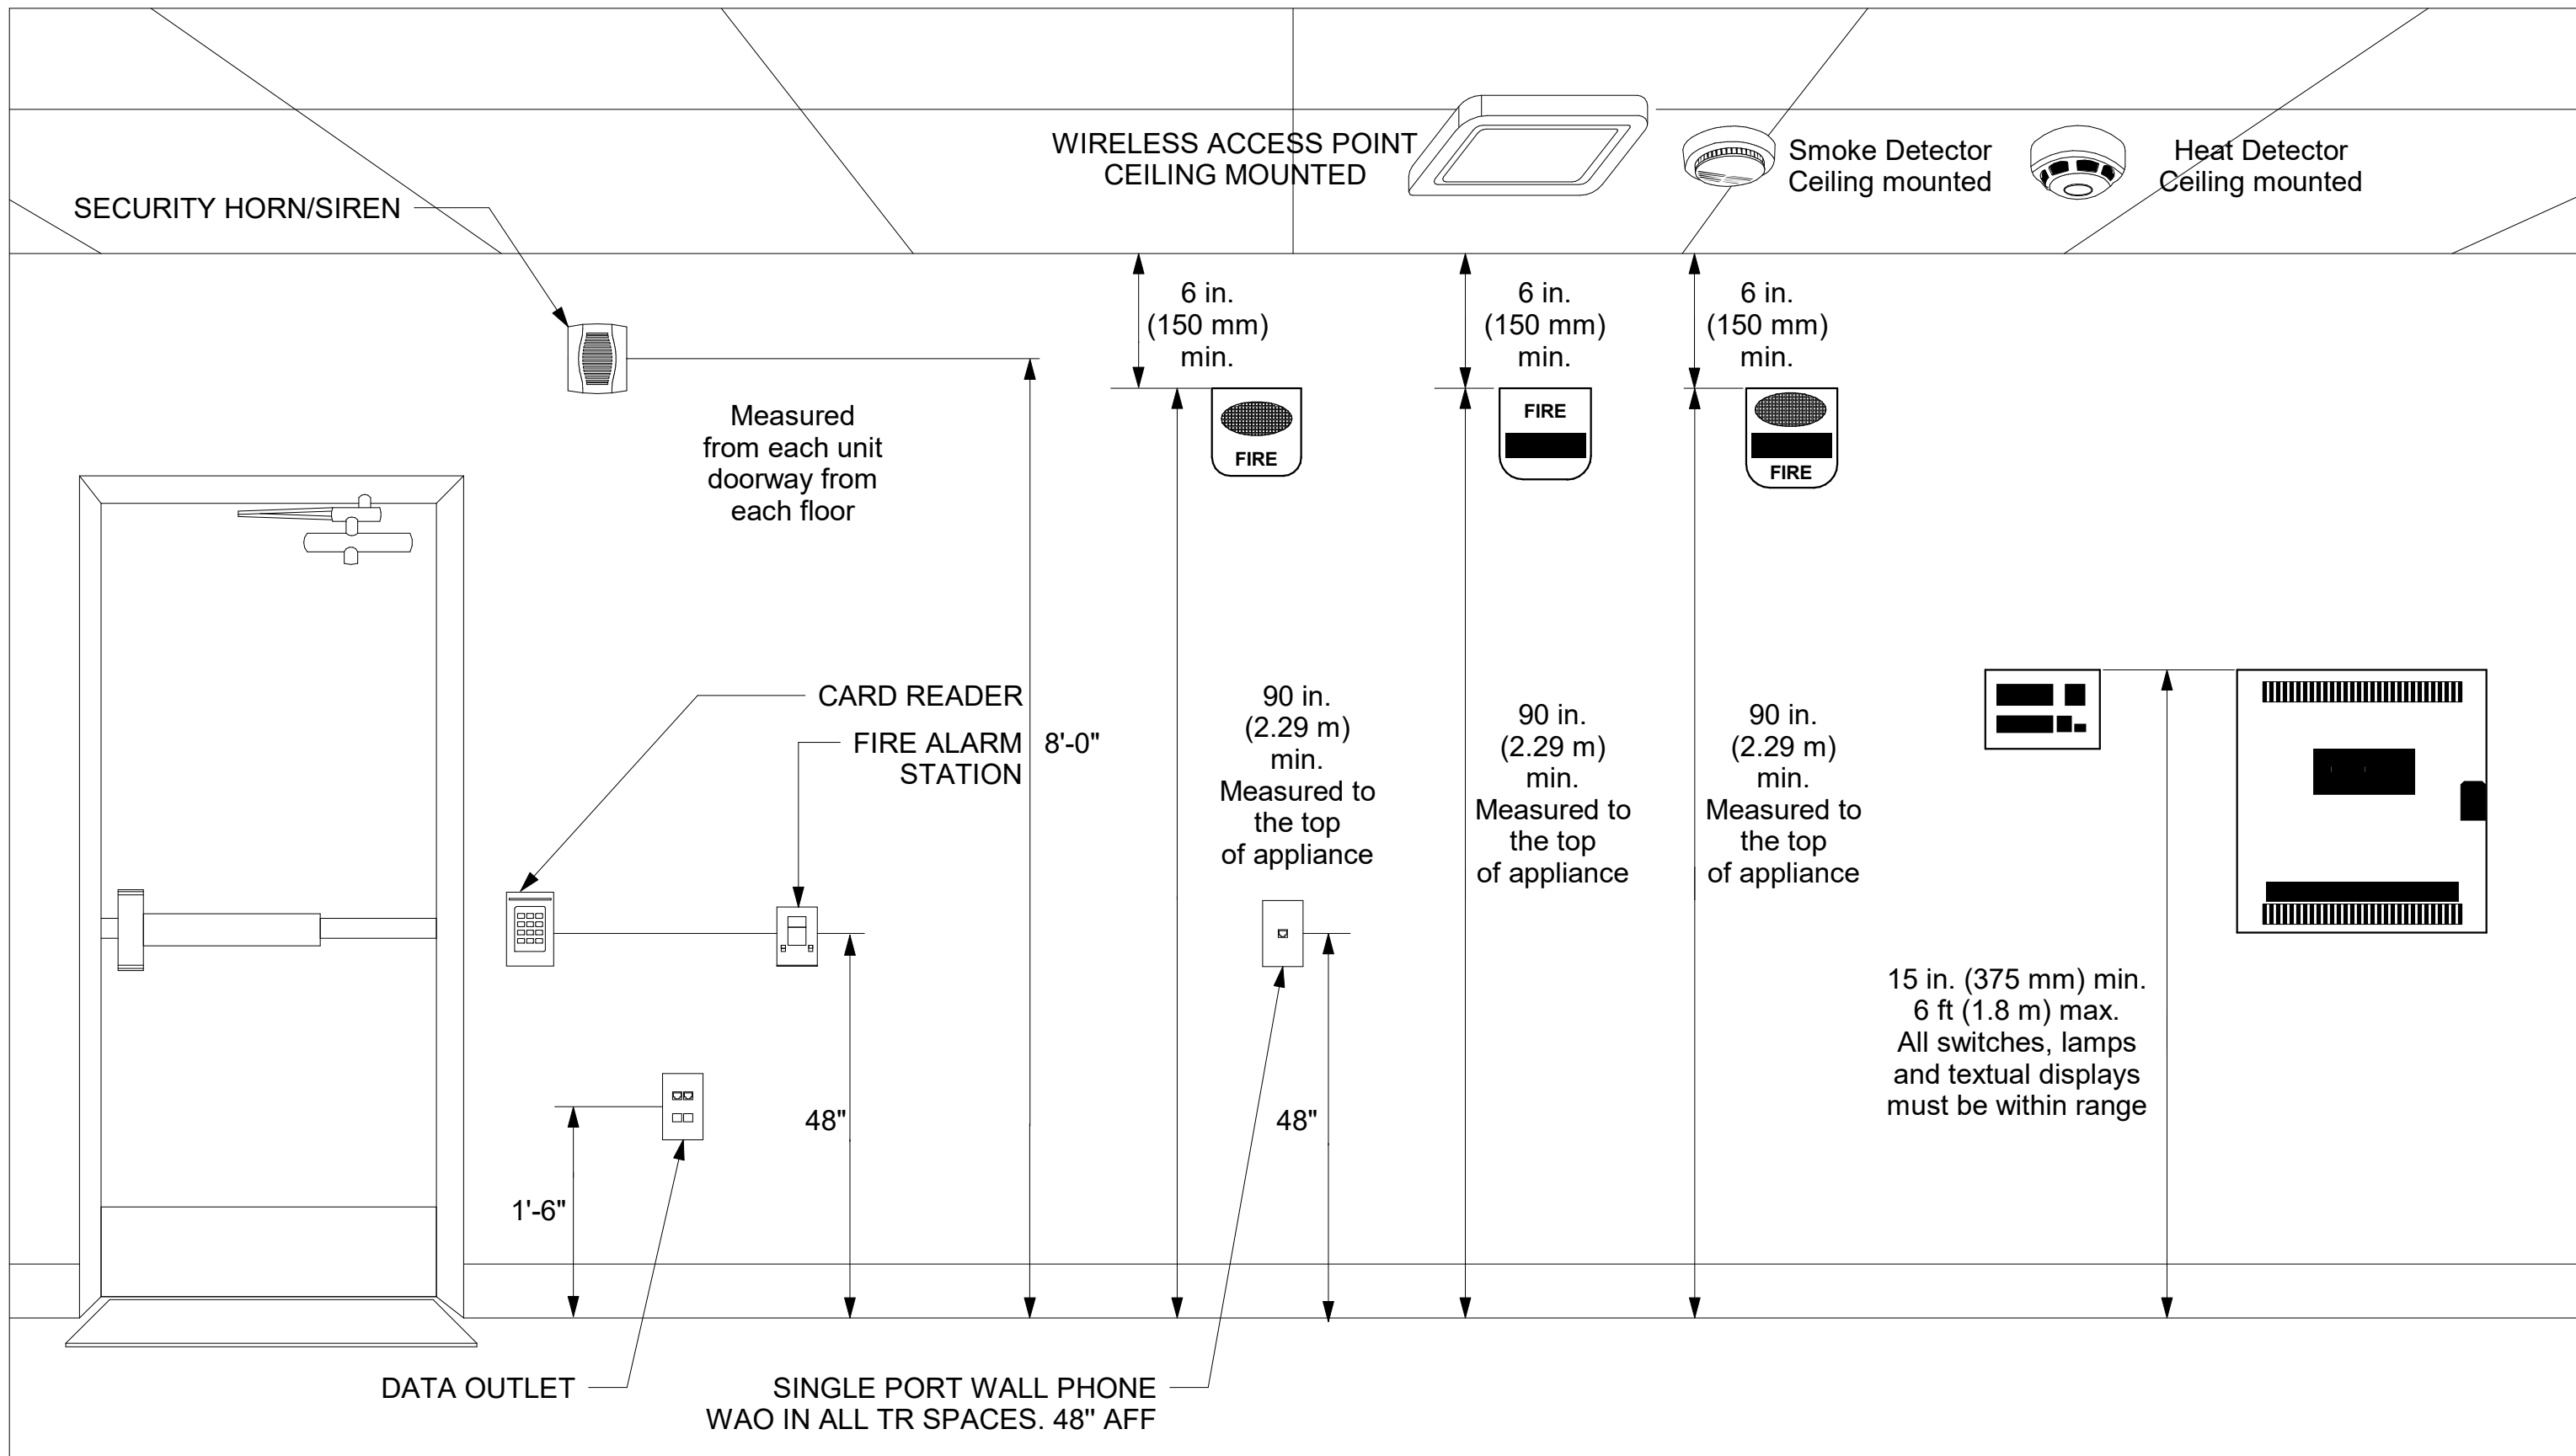

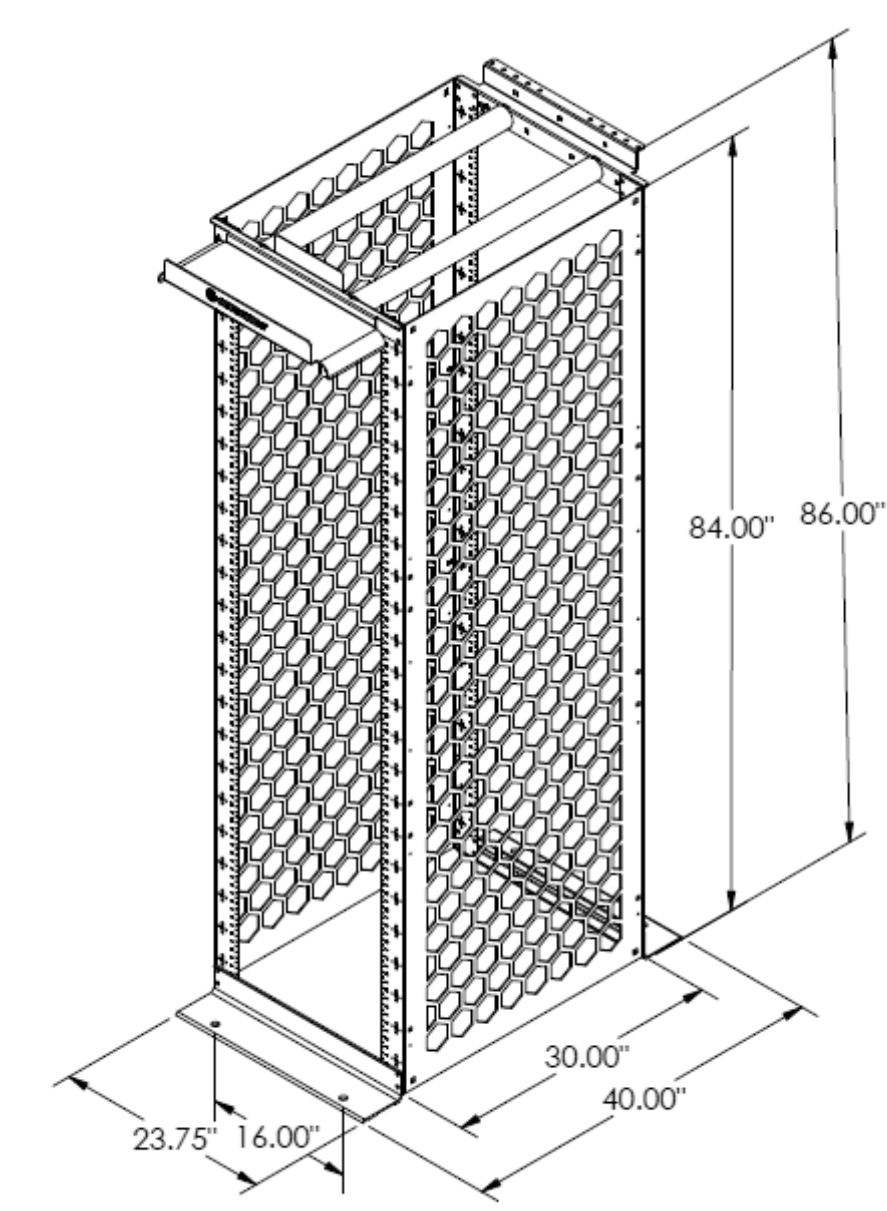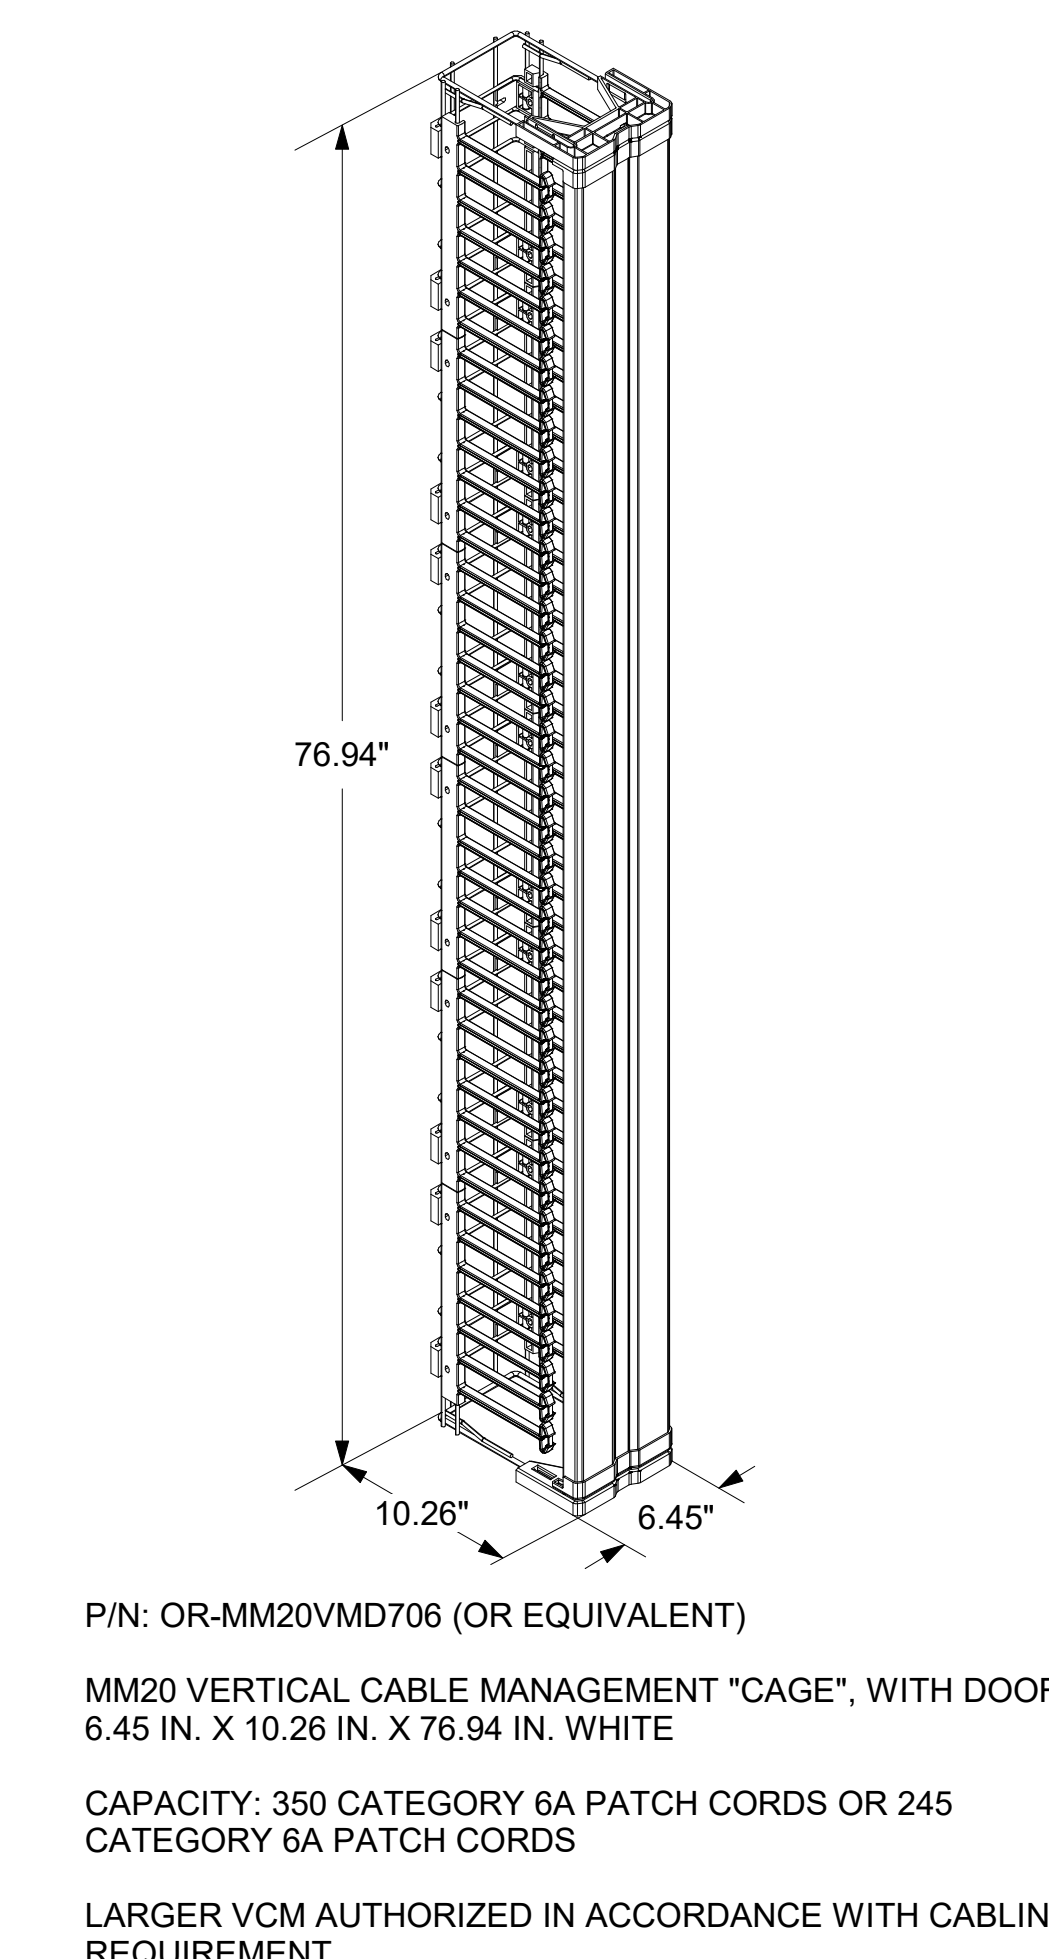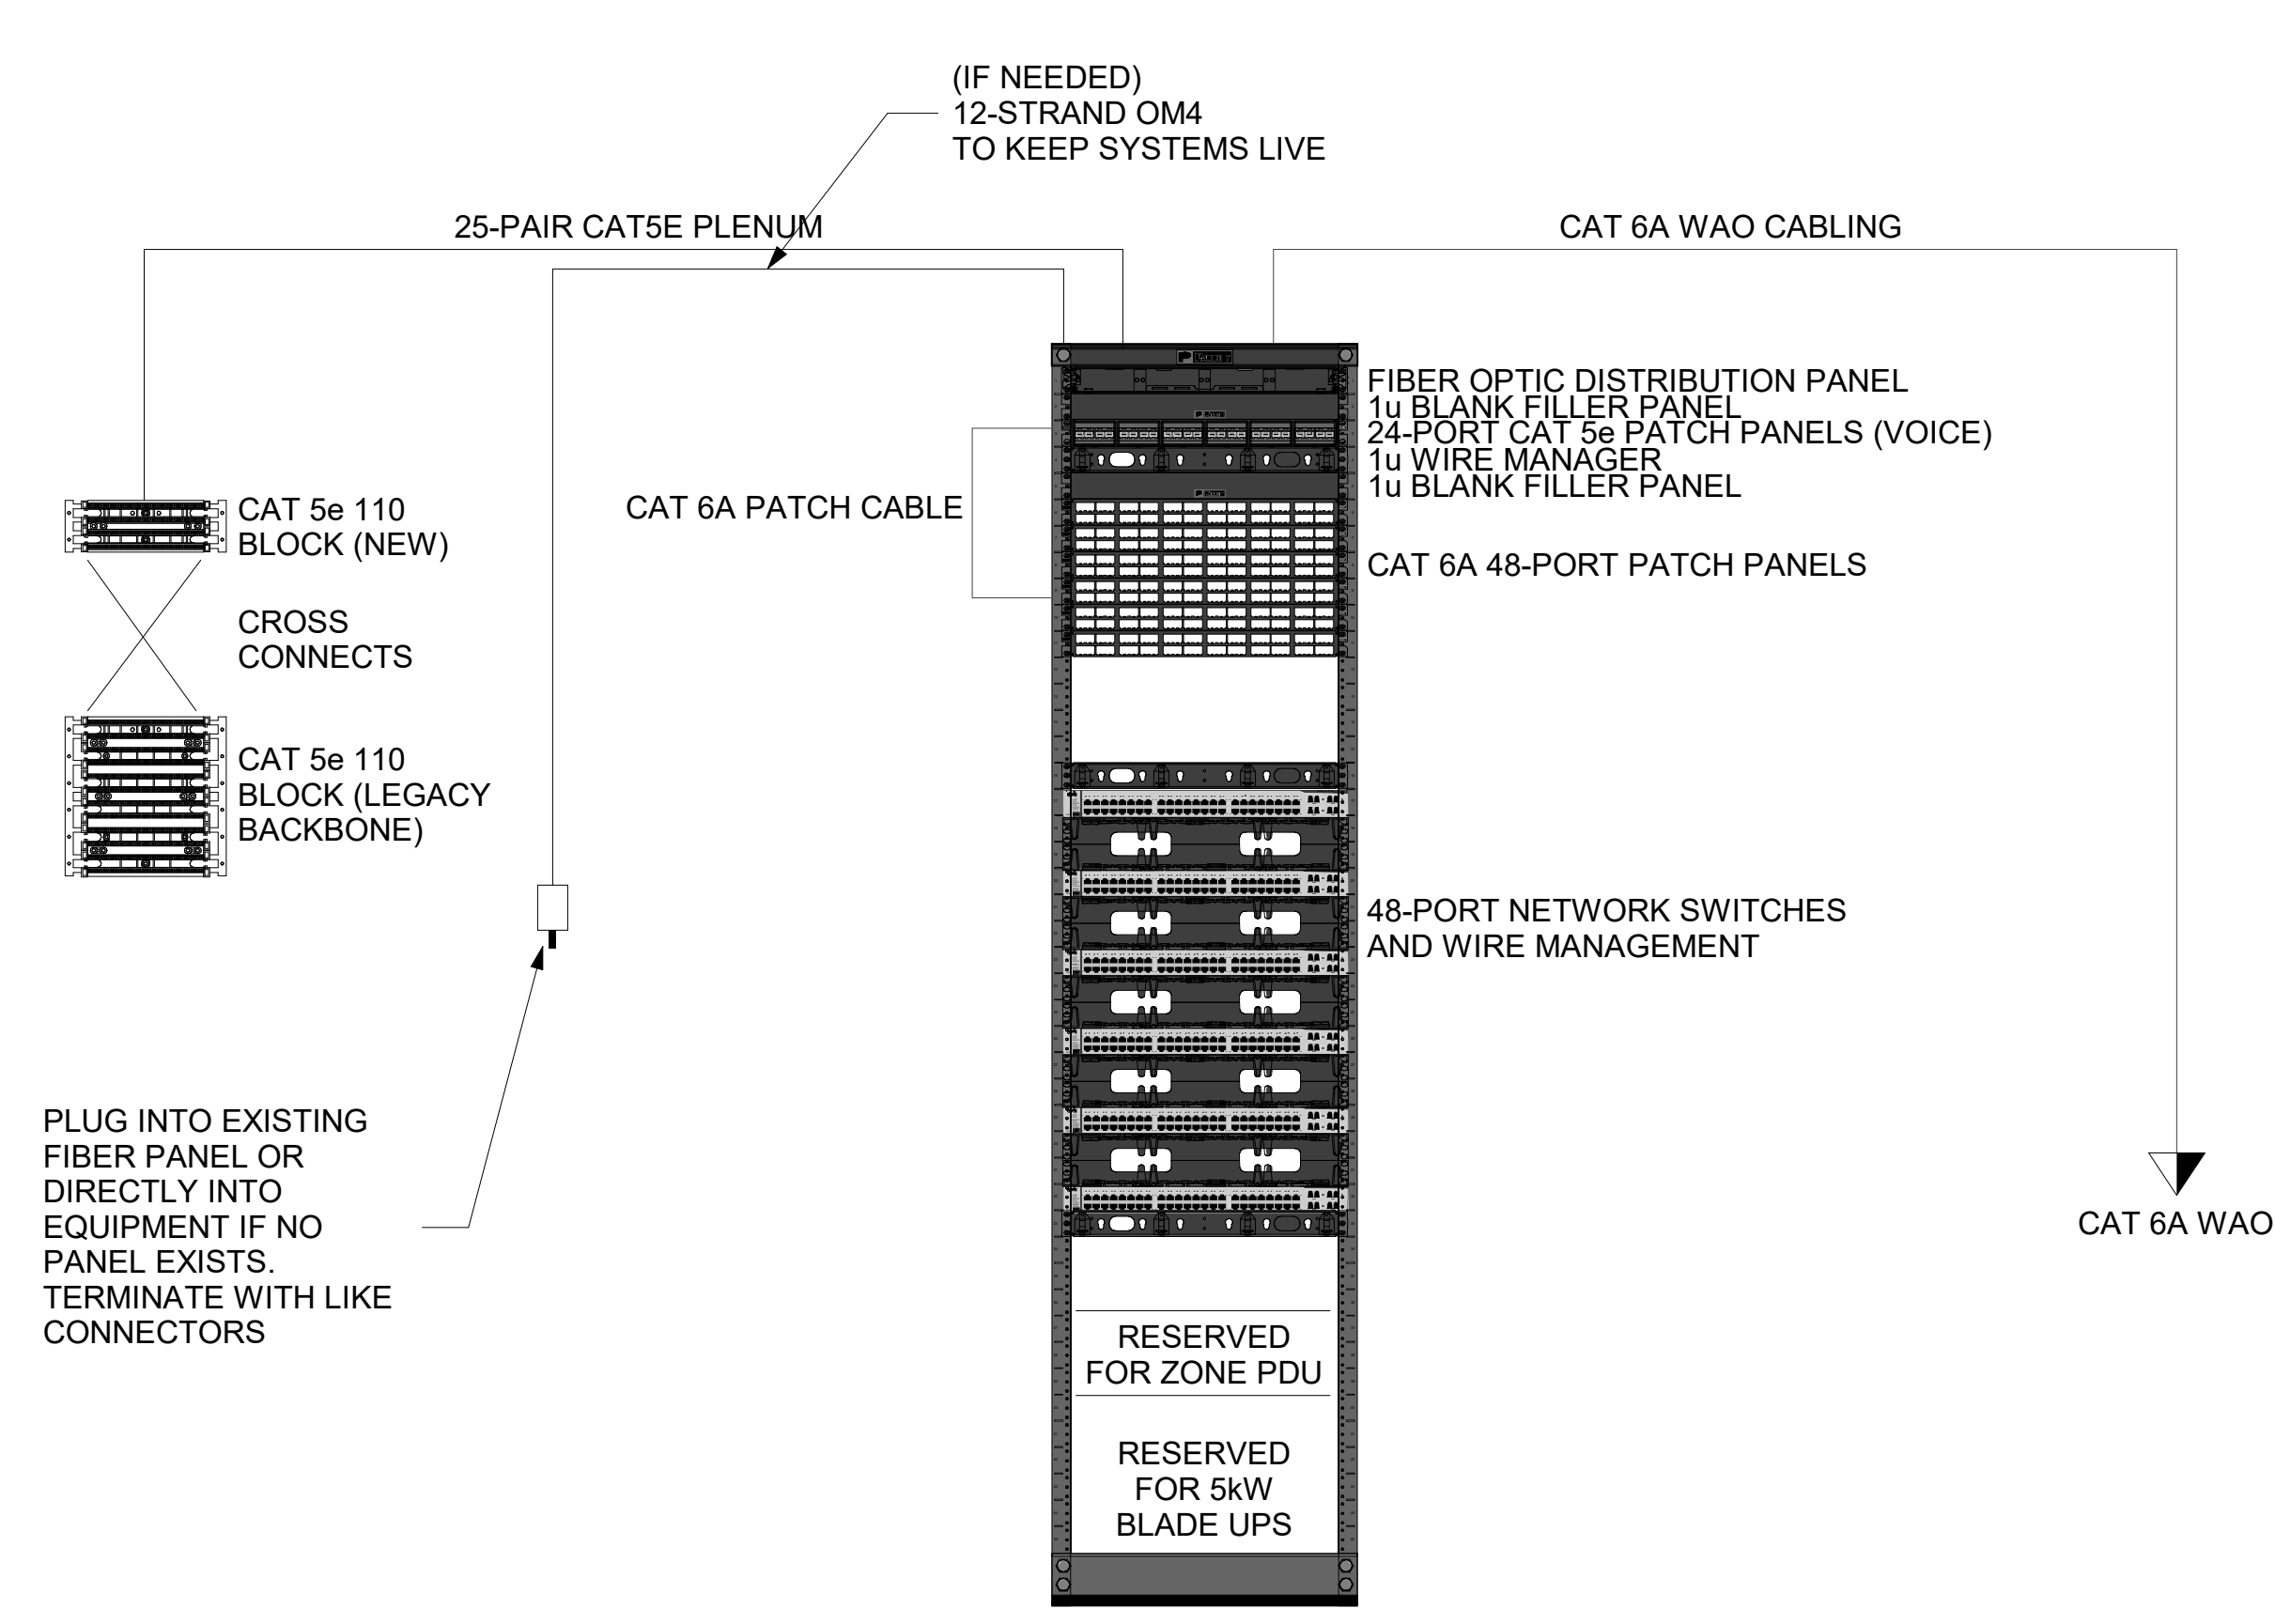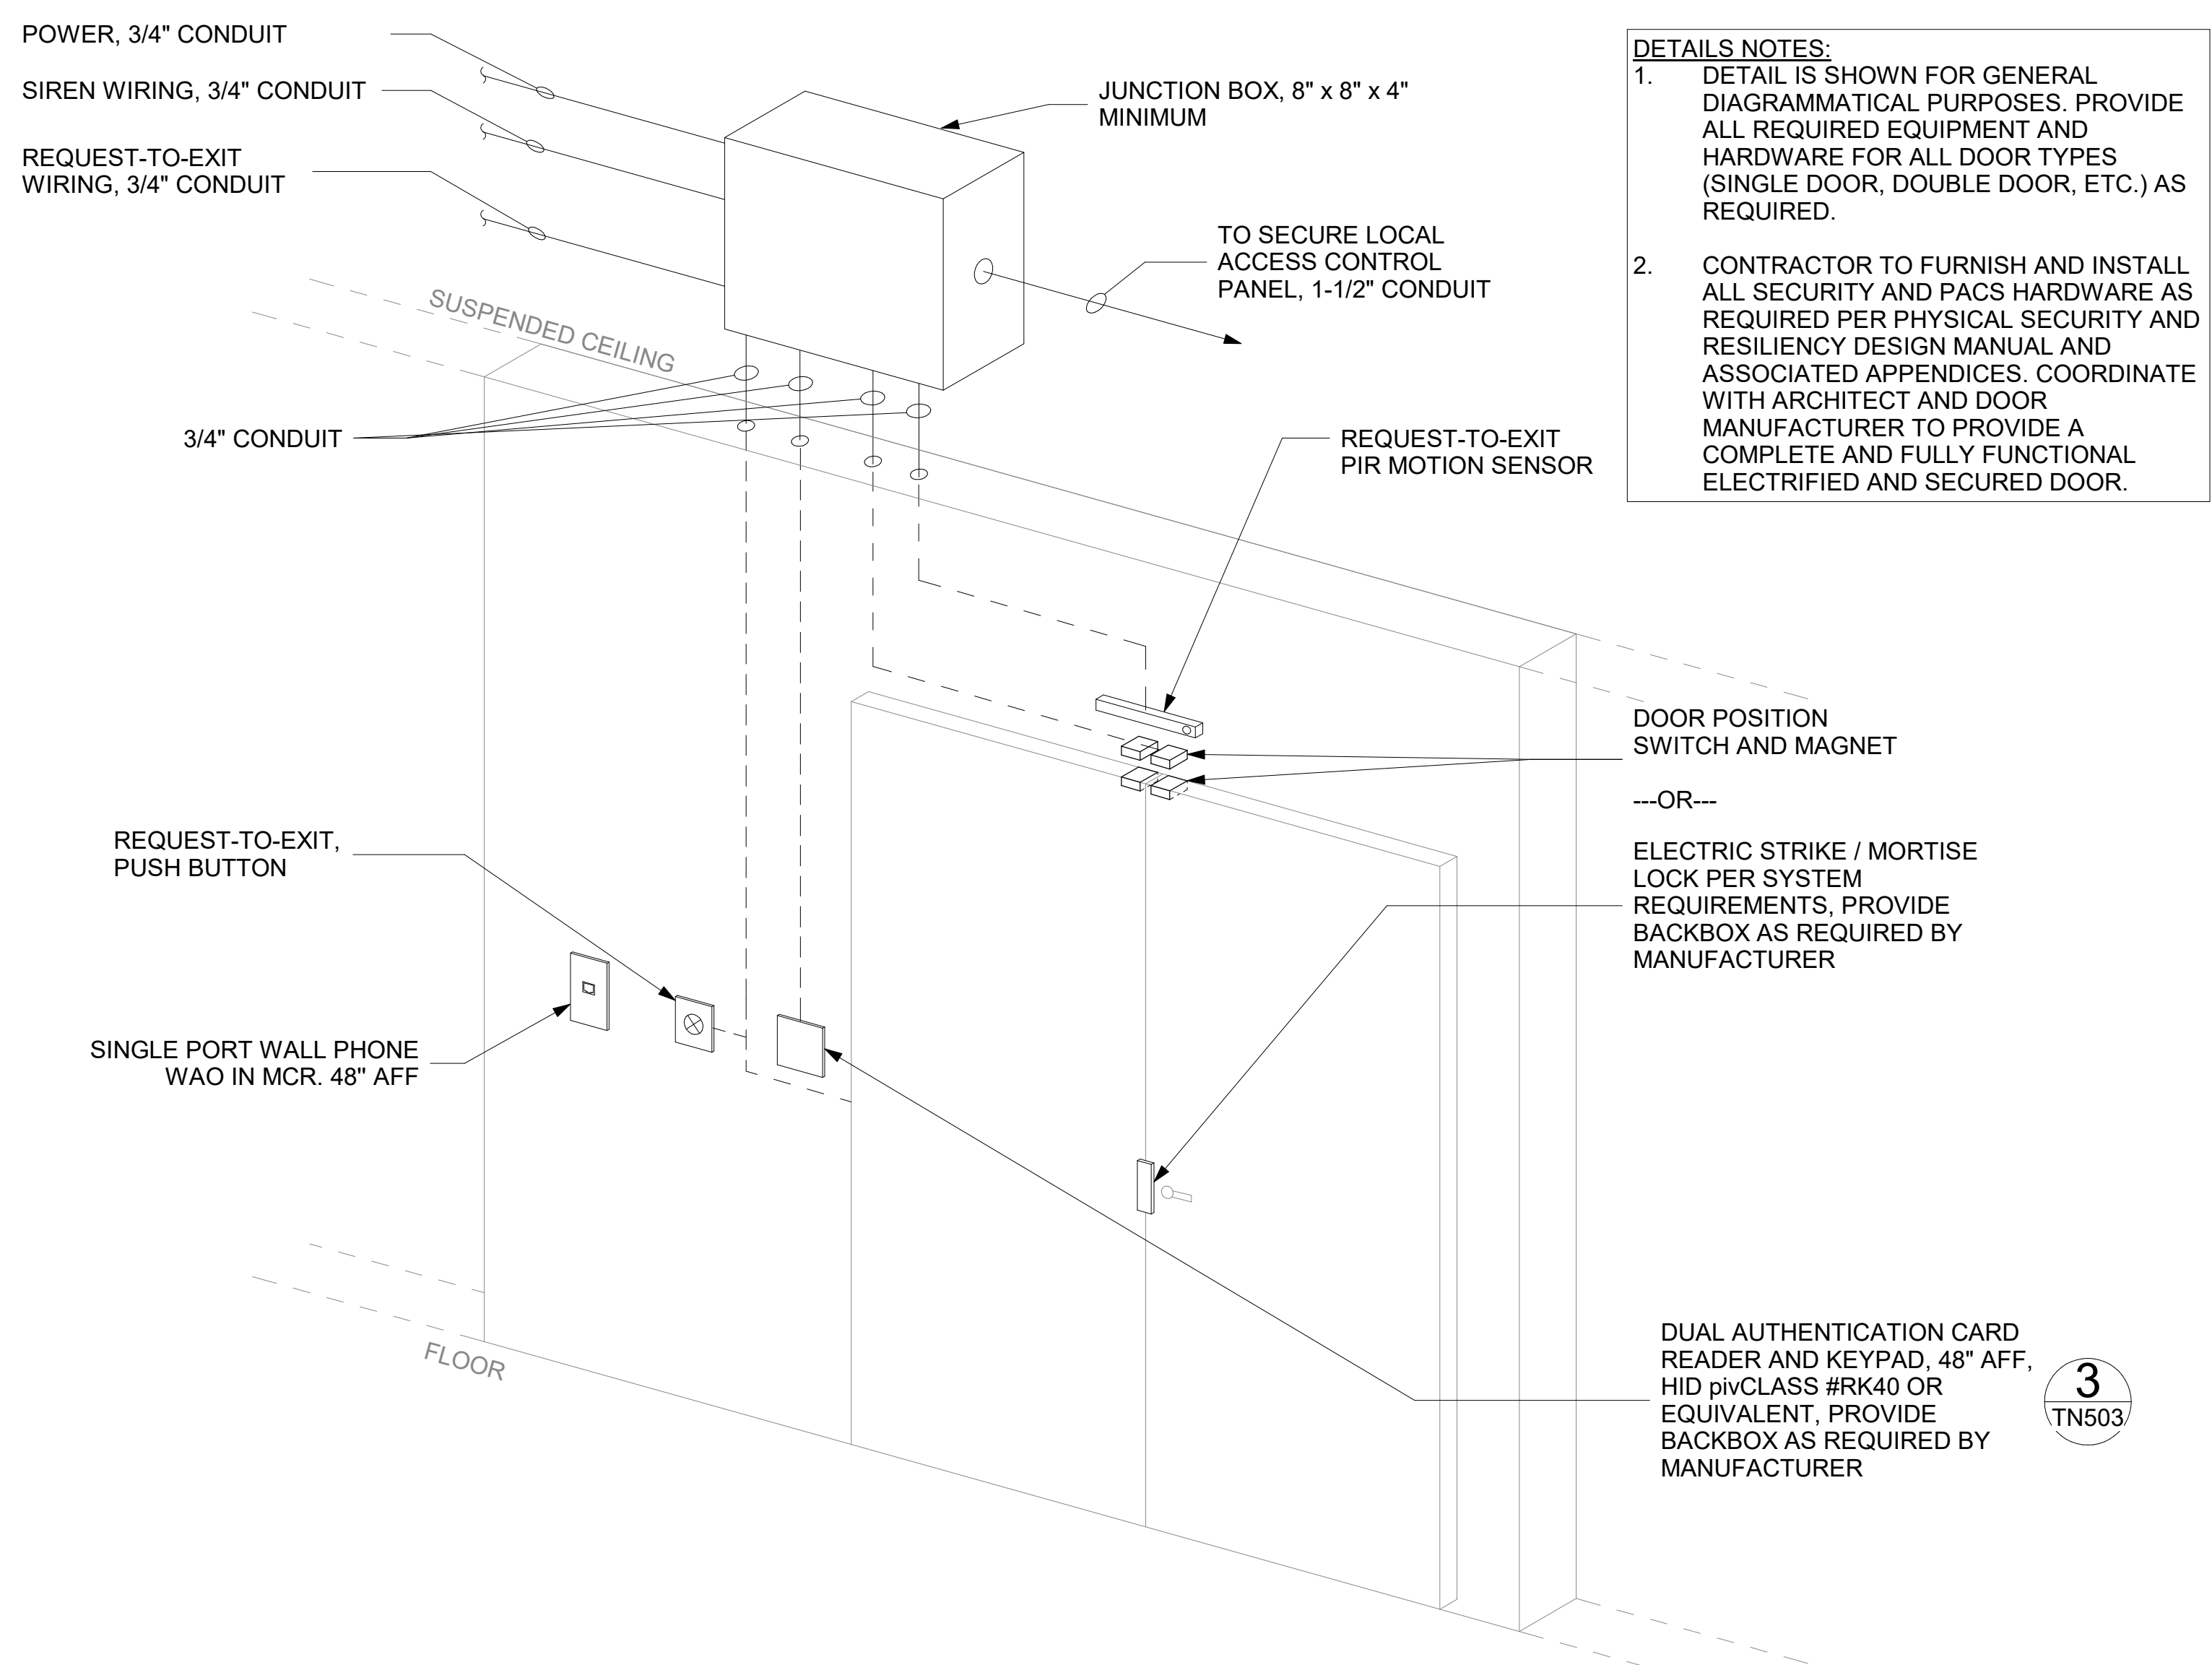


		CONSULTANT	ARCHITECT/ENGINEER OF RECORD	STAMP	Office of Construction and Facilities Management	Drawing Title	Phase	Project Title	Project Number	
		ENGINEERING DISCIPLINE:	A/E: SPEES DESIGN BUILD 23830 PACIFIC HIGHWAY S. SUITE 203 KENT, WA 98032			TELECOMMUNICATIONS DETAILS	100% CONSTRUCTION DOCUMENTS	EHRM INFRASTRUCTURE UPGRADES - HAMPTON	590-22-700	
						Approved:	FULLY SPRINKLERED	Location HAMPTON VA MEDICAL CENTER, HAMPTON, VIRGINIA	Building Number -	
								Issue Date 07/18/2025	Checked KG	Drawing Number TN506
									Drawn BCL/GPB	
										623 of 713
Revisions:	Date:				VA U.S. Department of Veterans Affairs					

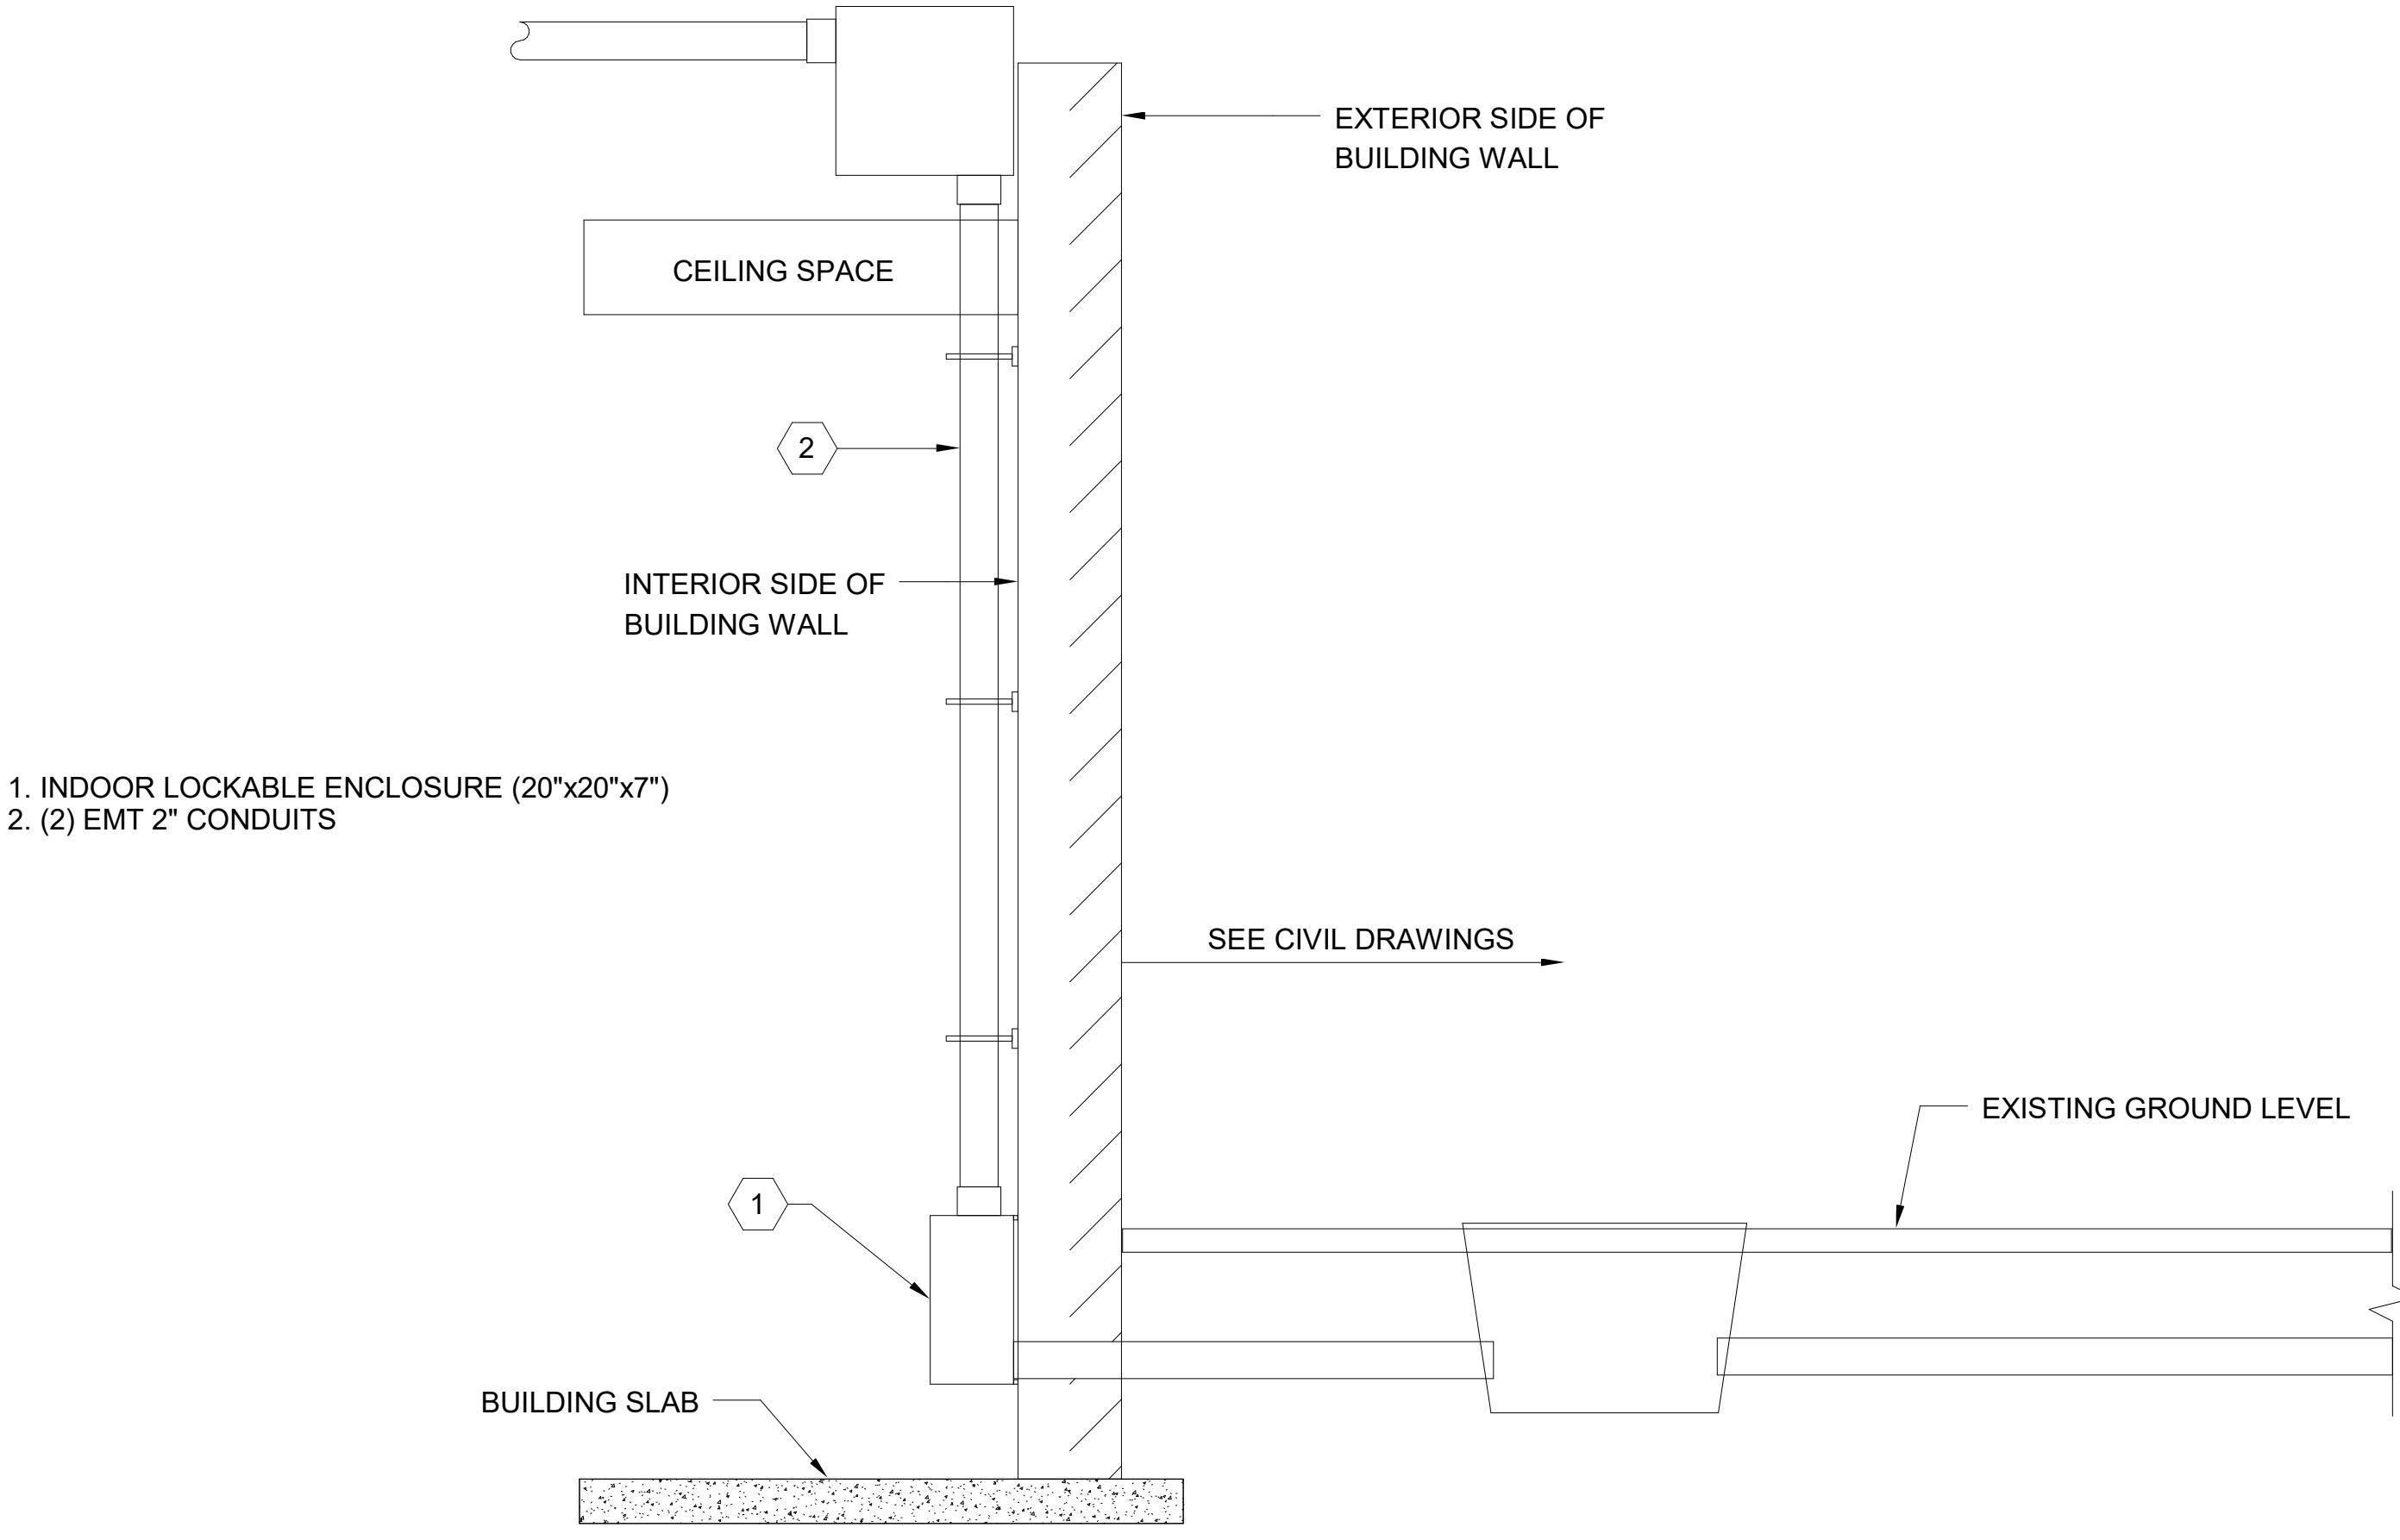1		2		3		4		5		6		7		8		9		10	
																			
1 NOT USED NTS										2 BELOW-GRADE BUILDING ENTRY DETAIL - TYPICAL NTS									
																			
3 NOT USED NTS										4 CAT6A SURGE PROTECTOR NTS									
Revisions:		Date:		CONSULTANT ENGINEERING DISCIPLINE:		ARCHITECT/ENGINEER OF RECORD A/E: SPEES DESIGN BUILD 23830 PACIFIC HIGHWAY S. SUITE 203 KENT, WA 98032 		STAMP 		Office of Construction and Facilities Management VA U.S. Department of Veterans Affairs		Drawing Title TELECOMMUNICATIONS DETAILS Approved:		Phase 100% CONSTRUCTION DOCUMENTS FULLY SPRINKLERED		Project Title EHRM INFRASTRUCTURE UPGRADES - HAMPTON Location HAMPTON VA MEDICAL CENTER, HAMPTON, VIRGINIA Issue Date 07/18/2025 Checked KG Drawn BCL/GPB		Project Number 590-22-700 Building Number - Drawing Number TN507 624 of 713	
1		2		3		4		5		6		7		8		9		10	

PHYSICAL SECURITY DEVICE SCHEDULE		DEVICE			
		Camera	Card Reader with Pin Pad	Motion Sensor	Request-to-Exit
ROOM TYPE	Telecommunications rooms (Note 1)	X	X	X	X

Notes:

1. Typical to all telecommunications rooms.

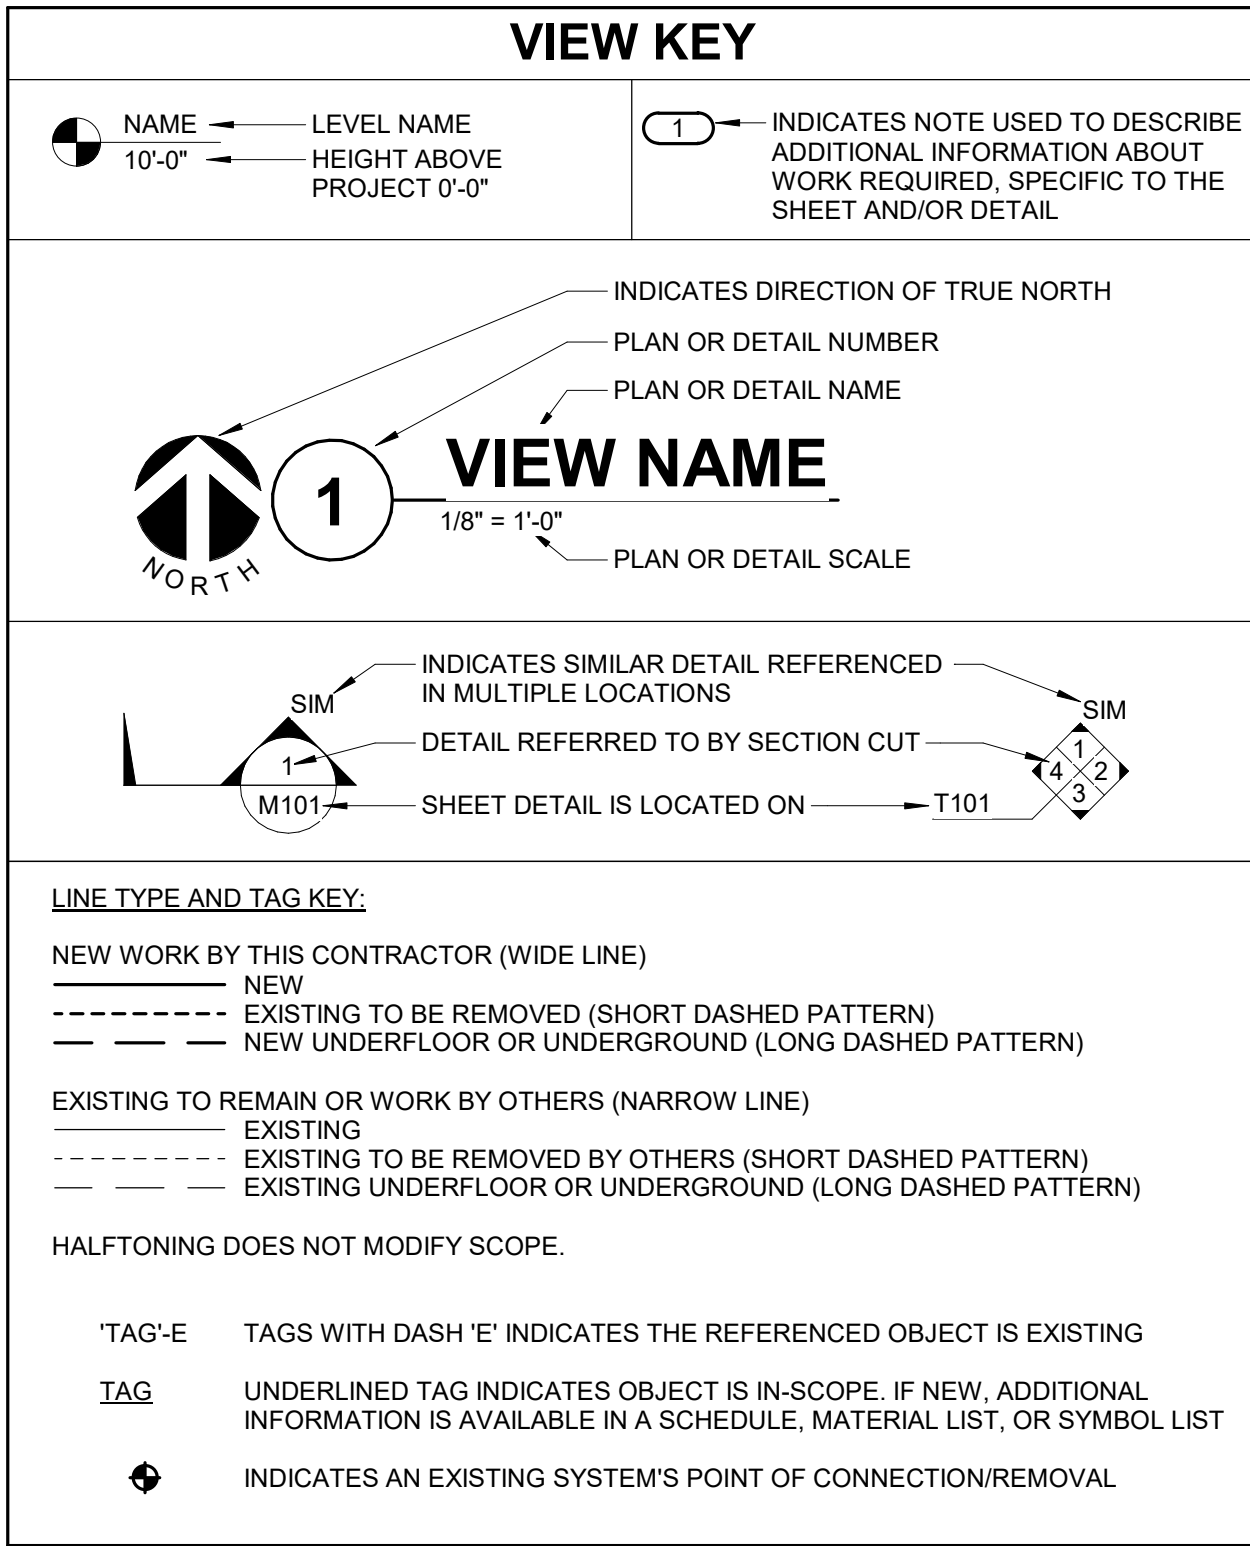

SUGGESTED MATRIX OF RESPONSIBILITY				
ITEM:	SHOWN ON:	FURNISHED BY:	INSTALLED BY:	NOTES:
TECHNOLOGY ROUGH-IN, REFER TO TECHNOLOGY EQUIPMENT SCHEDULE AND SPECIFICATIONS FOR DEFINITION CONDUIT SLEEVES (WHEN SHOWN ON DRAWINGS)	T-SERIES	E.C.	E.C.	3, 4.
CONDUIT SLEEVES (NOT SHOWN BUT REQUIRED FOR PROPER INSTALLATION OF SYSTEM)	N/A	E.C.	T.C.	2, 4.
TELECOMMUNICATION SYSTEMS ROUGH-IN	T-SERIES	E.C.	E.C.	1.
TELECOMMUNICATION EQUIPMENT, CABLING, AND TERMINATIONS	T-SERIES	T.C.	T.C.	
LOW VOLTAGE CABLING FOR TECHNOLOGY SYSTEMS	T-SERIES	T.C.	T.C.	
CABLE HANGERS AND SUPPORTS OR OTHER CABLE ROUTING METHODS (OTHER THAN CONDUIT AND CABLE TRAY)	T-SERIES	T.C.	T.C.	5.
TECHNOLOGY OUTSIDE PLANT CONDUITS, HANDHOLES, AND MANHOLES	T-SERIES	E.C.	E.C.	

- SUGGESTED MATRIX OF RESPONSIBILITY NOTES**
- LOCATIONS OF TELECOMMUNICATIONS ROUGH-INS SHALL BE INDICATED BY THE INFORMATION OUTLET SYMBOLS ON THE DRAWINGS. REFER TO THE TECHNOLOGY SYMBOL LIST FOR ADDITIONAL INFORMATION.
 - BASED ON THE INHERENT DIFFERENCES IN PRODUCTS FROM VARIOUS MANUFACTURERS, ALL REQUIRED EQUIPMENT MAY NOT BE SHOWN ON THE DRAWINGS FOR ALL ACCEPTABLE MANUFACTURERS.
 - INCLUDES BACKBOXES AND CONDUIT REQUIRED FOR THE TECHNOLOGY SYSTEMS INSTALLATION. THE E.C. SHALL BASE THE BID ON THE BASIS OF DESIGN SHOWN ON THE CONTRACT DOCUMENTS.
 - ALL CHANGES TO THE SLEEVES, BACKBOXES, CONDUITS, AND POWER REQUIRED BECAUSE OF THE T.C.'S SELECTION OF AN ALTERNATE ACCEPTABLE MANUFACTURER OR FROM SYSTEM CONFIGURATIONS THAT ARE LEFT TO THE CHOICE OF THE CONTRACTOR SHALL BE INCLUDED IN THE T.C.'S BID. THIS BID SHALL INCLUDE INSTALLATION BY A LICENSED ELECTRICIAN.
 - UNLESS TRADE RULES DICTATE OTHERWISE.

TECHNOLOGY SYMBOL LIST			
SYMBOL:	EQUIPMENT LIST ABBREV.:	DESCRIPTION:	NOTE:
	MHXX	PATHWAY TECHNOLOGY MANHOLE (FLOOR) TYPE 1	
	HHXX	PATHWAY TECHNOLOGY HANDHOLE (FLOOR) TYPE 1	
	WIDTH X HEIGHT	CABLE TRAY, CHANNEL TRAY, BASKET TRAY	
	WIDTH X HEIGHT	LADDER RACK	
	DIAMETERø C	CONDUIT	
		CONDUIT DOWN	
		CONDUIT UP	
		CONDUIT SLEEVE	
		CONTINUATION	
GENERAL NOTES:			
1. ALL SYMBOLS AND ABBREVIATIONS LISTED MAY NOT BE APPLICABLE TO THIS PROJECT. REFER TO THE TECHNOLOGY EQUIPMENT SCHEDULE FOR MORE COMPLETE DESCRIPTION AND ITEMS.			
2. ALL SYMBOLS AND ABBREVIATIONS REFER TO TECHNOLOGY SHEETS ONLY AS DEFINED ON THE SHEET INDEX. REFER TO THE GENERAL TECHNOLOGY NOTES FOR ADDITIONAL INFORMATION.			
3. ALL SYMBOLS LISTED ABOVE ARE FOR REFERENCE ONLY. REFER TO PLANS AND LINE TYPE KEY FOR NEW, EXISTING TO REMAIN AND TO BE REMOVED ITEMS FOR ADDITIONAL INFORMATION.			
4. REFER TO RISERS ON SHEET(S): T500, T501.			
TECHNOLOGY SYMBOL NOTES:			
1. REFER TO LINE TYPE KEY FOR NEW, EXISTING TO REMAIN, OR DEMO LINE TYPE.			
2. SYMBOL SUBSCRIPT INDICATES DEVICE TYPE. REFER TO TECHNOLOGY EQUIPMENT SCHEDULE 00-1000 FOR ADDITIONAL INFORMATION.			

CONTRACTOR ABBREVIATION KEY	
ABBR:	DESCRIPTION:
A.C.	ASBESTOS ABATEMENT CONTRACTOR
C.C.	CIVIL CONTRACTOR
C.M.	CONSTRUCTION MANAGER
E.C.	ELECTRICAL CONTRACTOR
F.P.C.	FIRE PROTECTION CONTRACTOR
G.C.	GENERAL CONTRACTOR
H.C.	HEATING CONTRACTOR
M.C.	MECHANICAL CONTRACTOR
P.C.	PLUMBING CONTRACTOR
S.C.	SECURITY CONTRACTOR
T.C.	TECHNOLOGY CONTRACTOR
T.C.C.	TEMPERATURE CONTROLS CONTRACTOR
V.C.	VENTILATION CONTRACTOR

TECHNOLOGY EQUIPMENT SCHEDULE		
THE EQUIPMENT LIST ABBREVIATIONS AND THE TECHNOLOGY EQUIPMENT SCHEDULE ARE FOR THE CONVENIENCE OF THE CONTRACTOR. EACH CONTRACTOR SHALL BE RESPONSIBLE FOR VERIFICATION OF QUANTITIES AND SHALL FURNISH ALL MATERIAL REQUIRED, WHETHER SPECIFIED OR NOT, TO PRODUCE A SATISFACTORY WORKING SYSTEM.		
CATALOG NUMBERS ARE NOT TO BE CONSIDERED COMPLETE BUT ARE GIVEN ONLY TO AID THE CONTRACTOR IN THE SEARCH FOR MATERIAL. NO MATERIAL SHALL BE ORDERED BY MANUFACTURER AND CATALOG NUMBER ONLY. EACH CONTRACTOR SHALL FIRST READ THE COMPLETE DESCRIPTION OF THE MATERIAL ON THESE DRAWINGS AND SPECIFICATIONS. THE FIRST MANUFACTURER LISTED IS THE BASIS OF DESIGN. "STANDARD COLOR" INDICATES FACTORY FINISH AVAILABLE AT NO ADDITIONAL CHARGE.		
EQUIPMENT LIST ABBREVIATION	EQUIPMENT LIST DESCRIPTION	MANUFACTURER AND MODEL
HH##	HANDHOLE COMPOSITE POLYMER CONCRETE BODY AND COVER. STAINLESS STEEL HARDWARE BOLTED NON-SKID COVER RATED FOR 15,000 LB DESIGN LOAD OCCASIONAL, NON-DELIBERATE VEHICULAR TRAFFIC. STACK UNITS TO ACHIEVE DEPTH SHOWN ON PLANS. UNITS IN LANDSCAPED AREAS SHALL BE GREEN IN COLOR. "COMMUNICATIONS" LOGO ON HANDHOLE COVER. CONTRACTOR SHALL FIELD VERIFY QUANTITY AND LOCATIONS. REFER TO 2000-1400 FOR DETAIL. PW-HH-1 = 24"Wx2'L.	HUBBELL/AQUAZITE PG2424ABH24 PG2424AH00 CARSON INDUSTRIES ARMORCAST HIGHLINE PRODUCTS SYNERTECH
MH##	PRE-CAST CONCRETE MAINTENANCE HOLE. AIR ENTRAINED 4000 PSI AASHTO HS-20; BRIDGE LOADING. MONOLITHIC CONSTRUCTION IN MODULAR SECTIONS WITH TONGUE AND GROOVE JOINTS. SQUARE RECTANGULAR SHAPE WITH TRUNCATED CORNERS 30 INCH DIAMETER CLEAR OPENING. REFER TO 00-1400 FOR ADDITIONAL INFORMATION INCLUDING SIZE.	OLD CASTLE PRE-CAST JENSEN PRE-CAST E.C. BABBERT
PW-PB-1	JUNCTION BOX, SURFACE MOUNT. SIZE PER N.E.C. SEE SPECIFICATIONS FOR GENERAL CONSTRUCTION, USE OF THIS SYMBOL DOES NOT INDICATE ALL JUNCTION BOXES REQUIRED FOR THIS CONTRACT ARE SHOWN.	SEE SPECIFICATIONS
SC-FDC-1	FIBER DISTRIBUTION CABINET - 19"W x 1.75"H x 17" DEEP, RACK MOUNTED ENCLOSURE, 1RMU, 16-GUAGE STEEL, POWDER-COATED BLACK FINISH, REMOVABLE TRANSPARENT HINGED DOOR, SLIDE-AWAY COVER, MOUNTING BRACKETS, REMOVABLE RUBBER GROMMETS, ACCEPTS SDX ADAPTER PLATE AND (3) MTP CASSETTES.	LEVITON #9R1UH-03 #5F100-S4L #5F100-16A OR APPROVED EQUAL
SC-FDC-2	FIBER DISTRIBUTION CABINET - 19"W x 3.50"H x 17" DEEP, RACK MOUNTED ENCLOSURE, 1RMU, 16-GUAGE STEEL, POWDER-COATED BLACK FINISH, REMOVABLE TRANSPARENT HINGED DOOR, SLIDE-AWAY COVER, MOUNTING BRACKETS, REMOVABLE RUBBER GROMMETS, ACCEPTS SDX ADAPTER PLATE AND (6) MTP CASSETTES.	LEVITON #9R2UH-06 #5F100-S4L #5F100-16A OR APPROVED EQUAL
SC-LR-1	LADDER RACK, 18" W TUBULAR STEEL CONSTRUCTION, RUST RESISTANT BLACK ENAMEL FINISH, U.L. LISTED, PROVIDE COMPLETE WITH ALL NECESSARY ADAPTERS, SUPPORT HARDWARE, AND FITTINGS, TO INCLUDE RADIUS DROPS. REMOVE SHARP BURRS FROM LADDER RACK AND REPAINT ALL AREAS THAT HAVE BEEN FIELD MODIFIED, CUT, OR EXPOSED	CHATSWORTH 10250-718 OR PRE-APPROVED EQUAL
SC-MDA-1	ENCLOSED CABINET, FLOOR MOUNT, 83.4"H x 40"W x 43.3"D, 19" PANEL MOUNTING, SQUARE PUNCHED CAGE NUT RAILS, 45RU, PERFORATED METAL FRONT DOOR WITH KEYPAD SWING HANDLE LOCK, DOUBLE PERFORATED METAL REAR DOOR WITH KEYPAD SWING HANDLE LOCK. PROVIDE WITH (2) SIDE PANELS WITH BRUSHED SEALED CABLE OPENINGS.	CHATSWORTH N-SERIES TERAPARAME GEN3: NFBN-114C-E42-1 (WHITE) SIDE PANELS: 39043-E63 OR EQUAL
SC-MPP-1	ANGELD MODULAR PATCH PANEL, (48) MODULAR HIGH-DENSITY CATEGORY 6A RJ45TERMINATIONS, MOUNTS DIRECTLY TO EIA/TIA STANDARD 19" RELAY RACK, PORT IDENTIFICATION NUMBER, PROVIDED WITH COLOR CODING AND LABEL HOLDER KITS, 1.75" MOUNTING SPACER, U.L. LISTED, PROVIDED WITH PANEL PANEL COVER AND REAR CABLE MANAGER.	LEVITON EZX1A-D48

TELECOM ROOM REFERENCES			
TELECOM ROOM	DETAIL / SHEET REFERENCE	FLOOR PLAN REFERENCE	ARCH ROOM NUMBER
TR #5A-7	1027-11-1400	07-11-T101	5A-7
TR #A51	1/13-1400	13-T201	A51
TR #A02A	1/14-1400	14-T201	A02A
TR#302A	1/15-1400	15-T201	302A
TE #108	1/17-1400	17-T201	108
TE #103	1/18-1400	18-T101	103
TR #109A	1/27-1400	27-T201	109A
TR# 204D	3/27-1400	27-T202	204D
TR #103B.1a	1/28-1400	28-T201	103B.1a
TR #106	1/31-1400	31-T201	106
TR #105	1/33-1400	33-T201	105
TR #1C	1/35-36-1400	35-36-T201	1C
TR #114	1/37-1400	37-T201	114
TR #105H	1/43-1400	43-T201	105H
TR #205H	4/43-1400	43-T202	205H
TR #105	1/44-1400	44-T101	103
TR #202	1/44-1401	44-T102	202
TE #110	1/48-1400	48-T202	110
TR #102A	1/66-1400	66-T201	102A
TR #202F	4/66-1400	66-T202	202F
TR #102	1/83-1400	83-T201	102
TR #SGC -1	1/110-1400	110-T200	SGC -1
TR #51C-1	3/110-1400	110-T201	51C1
TR #52C-1	5/110-1400	110-T202	52C-1
TR #53C-1	7/110-1400	110-T203	53C-1
TR #54D-1	1/110-1401	110-T204	54D-1
TR #C506	3/110-1401	110-T205	C506
TR #GA-157	1/108-1400	108-T201	GA-157
TR #2A-154A	4/108-1400	108-T203	2A-154A
TR #BG10	1/113-1400	113-T101	BG10
TR #AG1S5	3/113-1400	113-T101	AG1S5
TR #A114	1/114-1400	114-T101	A114
TR #103B	1/116-1400	116-T201	103B
TR #1C142	1/137-1401	137-T201	1C142
TR #B105B	3/137-1400	137-T201	B105B
TR #A85	1/137-1400	137-T201	A85
TR #C175	1/137-1401	137-T201	C175
TR #149	1/144-1400	144-T201	149
TR #251	4/144-1400	144-T202	251
TR #90A	3/146-1400	146-T201	90A
TR #3	1/146-1400	146-T201	3
TR #B185	4/148-1401	148-T101	B185
TR #C185	1/148-1401	148-T101	C185
TR #D185	1/148-1400	148-T101	D185
TR #A185	4/148-1400	148-T101	A185
TR #115	1/148T-1400	148T-1101	115
TR#10	1/168-1400	168-T201	10B
TR #61	1/173A-1400	173A-T201	61

TECHNOLOGY SHEET INDEX	
T-000	TECHNOLOGY COVERSHEET
TS-001	FACILITY SITE PLAN
7/11T-101	BLDG. 07.11 LEVEL 01 PLAN - TECHNOLOGY
7/11T-400	BLDG. 07.11 TECHNOLOGY DETAILS AND DIAGRAMS
13T-201	BLDG. 13 LEVEL 01 PLAN - TECHNOLOGY
13T-400	BLDG. 13 TECHNOLOGY DETAILS AND DIAGRAMS
14T-201	BLDG. 14 LEVEL 01 PLAN - TECHNOLOGY
14T-400	BLDG. 14 TECHNOLOGY DETAILS AND DIAGRAMS
15T-201	BUILDING 15-LEVEL 01 PLAN - TECHNOLOGY
15T-202	BUILDING 15-LEVEL 02 PLAN - TECHNOLOGY
15T-203	BUILDING 15-CATWALK LEVEL PLAN - TECHNOLOGY
14T-102	TECHNOLOGY ENLARGED PLANS
17T-201	BLDG. 17 LEVEL 01 PLAN - TECHNOLOGY
17T-400	BLDG. 17 TECHNOLOGY DETAILS AND DIAGRAMS
18T-101	BLDG. 18 LEVEL 01 PLAN - TECHNOLOGY
18T-400	BLDG. 18 TECHNOLOGY DETAILS AND DIAGRAMS
27T-200	BLDG. 27 BASEMENT PLAN - TECHNOLOGY
27T-201	BLDG. 27 LEVEL 01 PLAN - TECHNOLOGY
27T-202	BLDG. 27 LEVEL 02 PLAN - TECHNOLOGY
27T-400	BLDG. 27 TECHNOLOGY DETAILS AND DIAGRAMS
28T-201	BLDG. 28 LEVEL 01 PLAN - TECHNOLOGY
28T-400	BLDG. 28 TECHNOLOGY DETAILS AND DIAGRAMS
31T-100	BLDG. 31 BASEMENT PLAN - TECHNOLOGY
31T-101	BLDG. 31 LEVEL 01 PLAN - TECHNOLOGY
31T-400	BLDG. 31 TECHNOLOGY DETAILS AND DIAGRAMS
33T-201	BLDG. 33 LEVEL 01 PLAN - TECHNOLOGY
33T-400	BLDG. 33 TECHNOLOGY DETAILS AND DIAGRAMS
3538T-201	BLDG. 35-36 LEVEL 01 PLAN - TECHNOLOGY
3538T-400	BLDG. 35-36 TECHNOLOGY ENLARGEMENT PLANS
37T-201	BLDG. 37 LEVEL 01 PLAN - TECHNOLOGY
37T-400	BLDG. 37 TECHNOLOGY ENLARGEMENT PLANS
43T-201	BLDG. 43 LEVEL 01 PLAN - TECHNOLOGY
43T-202	BLDG. 43 LEVEL 02 PLAN - TECHNOLOGY
43T-400	BLDG. 43 TECHNOLOGY ENLARGEMENTS
44T-101	BLDG. 44 LEVEL 01 PLAN - TECHNOLOGY
44T-102	BLDG. 44 LEVEL 02 PLAN - TECHNOLOGY
44T-400	BLDG. 44 TECHNOLOGY ENLARGED PLANS
48T-201	BLDG. 48 LEVEL 01 PLAN - TECHNOLOGY
48T-202	BLDG. 48 LEVEL 02 PLAN - TECHNOLOGY
48T-400	BLDG. 48 TECHNOLOGY DETAILS AND DIAGRAMS
66T-201	BLDG. 66 LEVEL 01 PLAN - TECHNOLOGY
66T-202	BLDG. 66 LEVEL 02 PLAN - TECHNOLOGY
66T-400	BLDG. 66 TECHNOLOGY DETAILS AND DIAGRAMS
83T-201	BLDG. 83 LEVEL 01 PLAN - TECHNOLOGY
83T-400	BLDG. 83 TECHNOLOGY DETAILS AND DIAGRAMS
110T-200	BLDG. 110 LEVEL 02 PLAN - TECHNOLOGY
110B-201	BLDG. 110B LEVEL 01 PLAN - TECHNOLOGY
110B-202	BLDG. 110B LEVEL 02 PLAN - TECHNOLOGY
110B-400	BLDG. 110B TECHNOLOGY ENLARGED PLANS
110T-200	BLDG. 110 BASEMENT PLAN - TECHNOLOGY
110T-201	BLDG. 110 LEVEL 01 PLAN - TECHNOLOGY
110T-202	BLDG. 110 LEVEL 02 PLAN - TECHNOLOGY
110T-203	BLDG. 110 LEVEL 03 PLAN - TECHNOLOGY
110T-204	BLDG. 110 LEVEL 04 PLAN - TECHNOLOGY
110T-205	BLDG. 110 LEVEL 05 PLAN - TECHNOLOGY
110T-400	BLDG. 110 TECHNOLOGY ENLARGEMENTS
110T-401	BLDG. 110 TECHNOLOGY ENLARGEMENTS
113T-101	BLDG. 113 LEVEL 01 PLAN - TECHNOLOGY
113T-400	BLDG. 113 TECHNOLOGY ENLARGED PLANS
114T-101	BLDG. 114 LEVEL 01 PLAN - TECHNOLOGY
114T-102	BLDG. 114 LEVEL 02 PLAN - TECHNOLOGY
114T-400	BLDG. 114 TECHNOLOGY ENLARGED PLANS
116T-201	BLDG. 116 LEVEL 01 PLAN - TECHNOLOGY
116T-400	BLDG. 116 TECHNOLOGY ENLARGED PLANS
135T-200	BLDG. 135 LEVEL 00 - GROUND PLAN - TECHNOLOGY
135T-400	BLDG. 135 TECHNOLOGY ENLARGED PLANS
137T-201	BLDG. 137 LEVEL 01 PLAN - TECHNOLOGY
137T-400	BLDG. 137 TECHNOLOGY ENLARGED PLANS
137T-401	BLDG. 137 TECHNOLOGY ENLARGED PLANS
144T-101	LEVEL 01 PLAN - TECHNOLOGY
144T-102	LEVEL 02 PLAN - TECHNOLOGY
144T-400	TECHNOLOGY ENLARGED PLANS
146T-201	BLDG. 146 LEVEL 01 PLAN - TECHNOLOGY
146T-400	BLDG. 146 TECHNOLOGY ENLARGED PLANS
148T-101	BLDG. 148 LEVEL 01 PLAN - TECHNOLOGY
148T-400	BLDG. 148 TECHNOLOGY ENLARGED PLANS
148T-401	BLDG. 148 TECHNOLOGY ENLARGED PLANS
148T-101	BLDG. 148T LEVEL 01 PLAN - TECHNOLOGY
148T-400	BLDG. 148T TECHNOLOGY ENLARGED PLANS
168T-100	BLDG. 168 LEVEL 00 PLAN - TECHNOLOGY
168T-400	BLDG. 168 TECHNOLOGY ENLARGED PLANS
173A-201	BLDG. 173 LEVEL 01 PLAN - TECHNOLOGY
173A-400	BLDG. 173 TECHNOLOGY ENLARGED PLANS
T-400	TECHNOLOGY DETAILS
T-401	TECHNOLOGY DETAILS
T-500	TECHNOLOGY DIAGRAMS
T-301	TECHNOLOGY DIAGRAMS
GRAND TOTAL: 68	

FIRE / SMOKE BARRIER DESIGNATIONS	
THE LINE TYPES SHOWN ARE FOR THE CONVENIENCE OF THE CONTRACTOR. THE CONTRACTOR SHALL VERIFY RATINGS WITH THE LATEST SET OF ARCHITECTURAL PLANS AND FURNISH ALL MATERIALS REQUIRED TO COMPLY WITH THOSE RATINGS WHETHER SHOWN OR NOT.	
ALL [FLOOR, FLOOR CEILING, AND ROOF CEILING] ASSEMBLIES SHALL BE DESIGNATED AS [1], [2], [3], [4] HOUR FIRE (SMOKE) BARRIERS(S), UNLESS NOTED OTHERWISE ON THE PLANS. RATINGS WERE ACQUIRED FROM THE ARCHITECTURAL PLANS.	
FIRE PARTITION	-----
1 HOUR FIRE BARRIER	-----
2 HOUR FIRE BARRIER OR WALL	-----
3 HOUR FIRE BARRIER OR WALL	-----
4 HOUR FIRE BARRIER OR WALL	-----
SMOKE PARTITION	
SMOKE BARRIER	-----
1 HOUR FIRE/SMOKE BARRIER OR SHAFT ENCLOSURE	-----
2 HOUR FIRE/SMOKE BARRIER OR SHAFT ENCLOSURE	-----
3 HOUR FIRE/SMOKE BARRIER	-----
4 HOUR FIRE/SMOKE BARRIER	-----

TECHNOLOGY GENERAL NOTES:

- PW-CPW-1 INDICATES TECHNOLOGY EQUIPMENT SCHEDULE ITEM LABELED AS "EQUIPMENT LIST ABBREVIATION"
- REFER TO TECHNOLOGY EQUIPMENT SCHEDULE AND SPECIFICATIONS FOR FULL DESCRIPTIONS AND MANUFACTURERS OF ALL DEVICES.
- IF CONFLICT ARISES BETWEEN THE DRAWINGS AND SPECIFICATIONS, THE VA INFRASTRUCTURE STANDARD FOR TELECOMMUNICATIONS SPACES (ISTS) V4.0, PHYSICAL SECURITY AND RESILIENCY DESIGN MANUAL (VAPSRDM 2023) AND DIVISION 27/28 SPECIFICATIONS SHALL TAKE PRECEDENCE.

TECHNOLOGY MOUNTING SUBSCRIPT KEY:

A MOUNT AT +8" TO CENTERLINE ABOVE COUNTER OR BACKSPLASH

H MOUNT ORIENTED HORIZONTALLY

L MOUNT IN CASEWORK

M MOUNT IN MODULAR FURNITURE

S MOUNT IN SURFACE RACEWAY

A SLASH IS USED BETWEEN TWO SUBSCRIPTS, E.G., A/H.

TECHNOLOGY INSTALLATION NOTES:

- THE COMPLETE INSTALLATION SHALL BE IN ACCORDANCE WITH THE ADA STANDARDS FOR ACCESSIBLE DESIGN.
- CONCEAL ALL CONDUIT IN WALLS, PARTITIONS, ABOVE CEILING, IN FLOOR SLAB, ETC. UNLESS OTHERWISE INDICATED ON THE PLANS OR IN THE SPECIFICATIONS. CONDUIT IN MECHANICAL ROOMS AND STORAGE ROOMS WITHOUT CEILINGS MAY BE EXPOSED TO BUILDING STRUCTURE.
- TELECOMMUNICATIONS EQUIPMENT SHALL BE MOUNTED TO ALLOW ACCESS TO ELECTRICAL AND MECHANICAL EQUIPMENT. ALL MOUNTING OF TELECOMMUNICATION DEVICES ON EQUIPMENT SUPPLIED BY ANOTHER CONTRACTOR SHALL BE APPROVED IN ADVANCE BY THE OTHER CONTRACTOR.
- CONTRACTOR SHALL BE RESPONSIBLE FOR ALL OPENINGS REQUIRED IN WALLS. ALL OPENINGS SHALL BE REPAIRED TO MATCH EXISTING BY A QUALIFIED CONTRACTOR AT THE EXPENSE OF THIS CONTRACTOR. ALL CONDUITS THROUGH WALLS SHALL BE GROUTED OR SEALED INTO OPENINGS.
- ALL MATERIALS USED TO SEAL PENETRATIONS OF FIRE RATED WALLS AND FLOORS SHALL BE TESTED AND CERTIFIED AS A SYSTEM PER ASTM E814 STANDARDS FOR FIRE TESTS OF THROUGH-PENETRATION FIRESTOPPS. REFER TO DIVISION 7 FOR ADDITIONAL INFORMATION.
- THE TECHNOLOGY CONTRACTOR IS RESPONSIBLE FOR REMOVAL AND REPLACEMENT OF THE CEILINGS, CEILING TILES, AND CEILING GRID ASSOCIATED WITH THE AREAS OF WORK BY ALL CONTRACTORS. NOTIFY THE GENERAL CONTRACTOR OF AFFECTED AREAS PRIOR TO BIDDING.
- EACH CONTRACTOR IS RESPONSIBLE FOR DAMAGE CAUSED BY THEIR ACTIONS TO THE WALLS, FLOORS, AND ROOFS. THE CONTRACTOR WHOSE WORK CAUSES DAMAGE IS RESPONSIBLE FOR PATCHING TO MATCH ORIGINAL CONSTRUCTION, FIRE RATING, AND FINISH.

TECHNOLOGY PHASING NOTES

- THE EXISTING TELECOMMUNICATIONS BACKBONE TO REMAIN OPERATIONAL DURING THE INSTALLATION OF THE NEW TELECOMMUNICATIONS BACKBONE. THE SYSTEM SHALL NOT BE DISRUPTED UNLESS COORDINATED IN ADVANCE WITH THE OWNER AND ENGINEER AND AT THEIR DISCRETION ON DATE AND TIME.
- REFER TO THE DRAWINGS FOR THE LOCATIONS OF THE NEW TELECOMMUNICATIONS BACKBONE CABLING, PATHWAYS AND DATA CENTER. PORTIONS OF THE EXISTING BACKBONE PATHWAY SYSTEM SHALL BE MAINTAINED, ALL CABLING TO BE NEW WHEN THE EXISTING SYSTEM IS COMPLETE.
- REFER TO DRAWING T5001 FOR MCR AND BACKBONE PHASING REQUIREMENTS.

TECHNOLOGY OUTSIDE PLANT NOTES

- THE LOCATION OF THE CONDUIT, HAND HOLES AND/OR MAINTENANCE HOLES SHOWN ARE APPROXIMATE LOCATIONS. FIELD VERIFY THE LOCATION OF ALL UTILITIES PRIVATE AND/OR PUBLIC PRIOR TO THE INSTALLATION OF THE COMPONENT. FIELD COORDINATE THE FINAL LOCATION WITH THE OWNER AND ENGINEER PRIOR TO INSTALLATION.
- POTHOLES TO LOCATE EXISTING UNDERGROUND UTILITIES, IF APPLICABLE, SHALL BE IDENTIFIED AND REPAIRED PRIOR TO THE INSTALLATION OF THE COMPONENT. FIELD COORDINATE THE FINAL LOCATION WITH THE OWNER AND ENGINEER PRIOR TO INSTALLATION.
- HAND HOLES AND/OR MAINTENANCE HOLES SHALL BE CONSTRUCTED SO THAT THE TOP OF THE FRAME WILL BE FLUSH WITH THE GROUND LINE.
- REMOVAL AND REPLACEMENT OF THE EXISTING UNDERGROUND UTILITIES THAT ARE REQUIRED TO COMPLETE THE INSTALLATION SHALL BE INCLUDED IN THE CONTRACTOR'S BID.
- CONTRACTOR SHALL INCLUDE IN THEIR BID ANY REMOVAL AND REPLACEMENT OF EXISTING SIDEWALK, PAVEMENT, GRASS, SHRUBS, TREES, ETC. THAT WILL BE IMPACTED BY THE INSTALLATION OF THE NEW CONDUITS SHOWN ON THE DRAWINGS. IF TREES ARE REQUIRED TO BE REMOVED THE CONTRACTOR SHALL CONTACT THE OWNER AND DISCUSS OPTIONS PRIOR TO CUTTING DOWN ANY TREE OR SHRUB.
- NO ADDITIONAL COST SHALL BE APPROVED FOR PLACING CONDUITS DEEPER THAN REQUIRED MINIMUM DEPTH TO AVOID EXISTING UNDERGROUND UTILITIES.
- PROVIDE A MINIMUM OF 10'-0" SLACK LOOP WITHIN EACH HAND HOLE AND/OR 25'-0" FOR EACH MAINTENANCE HOLE. SLACK LOOP SHALL BE SECURE SO COPPER OR FIBER IS NOT RESTING ON EARTH AFTER FINAL INSTALLATION.

TECHNOLOGY ABBREVIATION KEY

ABBR:	DESCRIPTION:
AFF	ABOVE FINISHED FLOOR
AFG	ABOVE FINISHED GRADE
BFC	BELOW FINISHED CEILING
C	CONDUIT
DE	DELAYED EGRESS
DPOT	DOUBLE POLE DOUBLE THROW
FOV	FIELD OF VIEW
J-BOX	JUNCTION BOX
POE	POWER OVER ETHERNET
PTZ	PAN TILT ZOOM
SIM	SIMILAR
TYP	TYPICAL
UON	UNLESS OTHERWISE NOTED
+	MOUNTING HEIGHT ABOVE FINISHED FLOOR
TR-#	TELECOMMUNICATIONS ROOM
TE-#	TELECOMMUNICATIONS ENCLOSURE
MCR	MAIN COMPUTER ROOM

Revisions:	Date:

A

B

C

D

E

F

CAMPUS SITE OPTICAL FIBER BACKBONE CABLE LEGEND	
DESIGNATION	DESCRIPTION OF CABLES IN CONDUITS
(##) A	QTY. OF A-LOOP 24-STRAND OS2 CABLES.
(##) A1	QTY. OF A-LOOP 24-STRAND OM4/ 12-STRAND OS1 HYBRID CABLES.
(##) B	QTY. OF B-LOOP 24-STRAND OS2 CABLES.
(##) B1	QTY. OF B-LOOP 24-STRAND OM4/ 12-STRAND OS1 HYBRID CABLES.

NOTES:

1. CONTRACTOR SHALL BE SOLELY RESPONSIBLE FOR PERFORMING A DETAILED TAKE-OFF AND VERIFYING ALL OPTICAL FIBER CABLING QUANTITIES, ROUTES, AND CONFIGURATIONS INDICATED ON THE DRAWINGS. VERIFICATION MUST BE COMPLETED PRIOR TO BID SUBMISSION, MATERIAL PROCUREMENT, AND INSTALLATION.



- GENERAL NOTES:**
- MAXIMUM DISTANCE BETWEEN MANHOLES AND HAND HOLES SHALL BE 400 FEET.
 - LATERAL PATHWAYS FROM THE CAMPUS MAIN LOOPS TO INDIVIDUAL BUILDINGS SHALL CONSIST OF TWO (2) 4" CONDUITS. PROVIDE TWO (2) DIVERSE PATHS FOR CLINICAL BLDGS.
 - REFER TO INDIVIDUAL BUILDING FLOOR PLANS FOR ENTRANCE LOCATIONS OF PATHWAYS A AND B INTO THE BUILDING. REFER TO BUILDINGS 135 AND BUILDING 110 ON SITE PLAN FOR START OF A-LOOP AND B-LOOP DUCTBANK ROUTING.
 - REFER TO T-401 FOR DUCTBANK DETAILS.
 - REFER TO T-401 FOR EXTERIOR WALL MOUNTED PULLBOX DETAILS.
 - PROVIDE (3) #MVE5224 MAXCELL 4-CELL FABRIC INNERDUCTS IN EACH 4" CONDUIT.
 - CORE A AND CORE B DUCTBANKS ARE IN COMMON TRENCH FOR MAIN CAMPUS OPTICAL FIBER CABLE LOOP.
 - NEW BACKBONE OPTICAL FIBER CABLE JACKETS SHALL BE INDOOR/OUTDOOR RATED.
 - ALL BACKBONE OPTICAL FIBER CABLE PATHWAYS SHALL BE NEW. DO NOT RE-USE EXISTING BACKBONE CABLE PATHWAYS FOR NEW BACKBONE CABLES.
 - ALL EXISTING COPPER VOICE BACKBONE CABLES TO REMAIN. PROTECT IN PLACE.
 - AFTER REMOVAL OF EXISTING OPTICAL FIBER BACKBONE CABLES FROM OUT-BUILDING TR BACK TO EXISTING MAIN COMPUTER ROOM IN BLDG #135, CREATE A CABLE SCHEDULE OF REMAINING ACTIVE BACKBONE CABLES IN EXISTING UNDERGROUND DUCTBANKS. SCHEDULE SHALL INCLUDE CABLE TYPES, QUANTITIES, PATHWAY SIZE, AND AVAILABLE CAPACITY.

- KEY NOTES: (B)**
- PROVIDE (6) 4" CONDUITS FOR CORE A AND CORE B BETWEEN ALL MANHOLES ON CAMPUS NEW MAIN BACKBONE FIBER LOOP.
 - MANHOLE, TYPE MHXX, REFER TO DETAIL 1/T400. "XX" REPRESENT NUMBERING OF MANHOLE ON CAMPUS FIBER LOOP.
 - HANDHOLE, TYPE HHXX, REFER TO DETAIL 2/T400. "XX" REPRESENT NUMBERING OF HANDHOLE ON CAMPUS FIBER LOOP.
 - APPROXIMATE LOCATION OF EXISTING SERVICE PROVIDERS (SP1 AND SP2) UNDERGROUND CONDUIT DUCTBANK ROUTE BETWEEN BUILDINGS AND EXISTING MAIN COMPUTER ROOM (MCR).
 - PROVIDE (2) 4" DUCTBANK WITH MAXCELL CELL PACK AND ROUTE FROM EXISTING SP2 MANHOLE INTO COMMON TRENCH WITH NEW FIBER DUCTBANK LOOP.
 - LOCATION OF B-LOOP AND SP2 CONDUIT ENTRY INTO BUILDING 110. REFER TO BUILDING 110 PLANS FOR CONTINUATION.
 - ROUTE NEW A-LOOP CONDUITS BELOW GRADE OUT OF BLDG #135 NEAR TO EXISTING TELECOM CONDUIT DUCTBANK ROUTE BETWEEN BLDG #135 AND #116. MAINTAIN SEPARATION BETWEEN DUCTBANKS AND DO NOT DISTURB EXISTING CONDUIT DUCTBANK DURING ROUTE OF NEW CONDUIT DUCTBANK. REFER TO BLDG 135 PLANS FOR CONTINUATION OF CONDUIT ROUTE IN BLDG 135.
 - ADD NEW 4" CONDUITS INTO DUCTBANK LOOP AT MANHOLE MH15 WITH CONDUITS ROUTED WEST.
 - BUILDINGS #60, #65 SHALL RECEIVE DUCTBANKS AND HANDHOLES WITH 100'FT OF COILED FIBER LOOP SLACK PER HANDHOLE. PROVIDE WEATHERPROOF BAG TO PROTECT FIBER LOOP SLACK IN HANDHOLE.
 - LOCATION OF SERVICE PROVIDER SP1 EXISTING SITE UTILITY POLE. CONTRACTOR SHALL PROVIDE (2) 4" CONDUITS STUBBED UP AT BASE OF POLE AND EXTEND TO NEW HANDHOLE. PROVIDE ADDITIONAL (2) 4" DUCTBANK FROM NEW HANDHOLE TO EXISTING MANHOLE IN PARKING LOT.
 - PROVIDE 4" DUCTBANK FROM EXISTING MANHOLE AND ROUTE INTO COMMON TRENCH WITH NEW CAMPUS DUCTBANK LOOP. CONTINUE ROUTE OF SP1 CONDUITS INTO BLDG #135.
 - ROUTE CAMPUS NEW MAIN FIBER DUCTBANK LOOP THROUGH CRAWL SPACE OF BLDG #146. PROVIDE CONDUITS FROM MAIN DUCTBANK TO TR IN BLDG 146. CORE A AND CORE B LATERALS TO BLDG 146. REFER TO BLDG 146 FLOOR PLAN FOR ADDITIONAL WORK REQUIREMENTS. REFER TO 4/T400 FOR DUCTBANK DETAILS.


- VA HAMPTON EHRM - MAIN COMPUTER ROOM (MCR) PHASING SEQUENCE**
- PHASE 1 - CAMPUS INFRASTRUCTURE**
- INSTALL NEW DUCTBANK SYSTEM AND NEW BACKBONE OPTICAL FIBER CABLE PULLS.
- PHASE 2 - CAMPUS BACKBONE CABLING**
- PULL NEW OPTICAL FIBER CABLES THROUGH DUCTBANKS AND BUILDING TO EXISTING, EXPANDED OR NEW TRs.
 - IN BUILDINGS, TERMINATE NEW OPTICAL FIBER CABLES IN NEW FIBER ENCLOSURES IN NEW RACKS.
 - IN EXISTING MCR, TERMINATE NEW OPTICAL FIBER CABLES IN NEW FIBER ENCLOSURES IN NEW FIBER DISTRIBUTION CABINETS.
 - TEST NEW OPTICAL FIBER CABLES.
 - VA TO PROVIDE UP TO (10) TEN NETWORK SWITCHES TO MITIGATE DOWNTIME DURING TRANSITION FROM OLD MCR TO NEW MCR.
- PHASE 3 - ACTIVATE OPTICAL FIBER IN EXISTING/NEW TRs**
- ACTIVATE OPTICAL FIBER CABLES IN NEW TRs.
 - EXISTING/EXPANDED TRs - PROVIDE NEW FIBER JUMPERS FROM NEW FIBER ENCLOSURE BACK TO EXISTING NETWORK SWITCHES. DISCONNECT AND REMOVE EXISTING FIBER CABLES COMPLETE.
 - NEW TRs - PROVIDE TEMPORARY FIBER BACKFEED TO EXISTING TR LOCATION AND PATCH INTO EXISTING NETWORK SWITCHES. DISCONNECT AND REMOVE EXISTING FIBER CABLES COMPLETE.
 - ONCE ALL NEW OPTICAL FIBER CABLES HAVE BEEN ACTIVATED INTO ALL NEW AND EXISTING TRs ON THE NEW CORE SWITCH IN EXISTING MCR, THE EXISTING CORE SWITCH CAN BE RELOCATED TO NEW DISTRIBUTION CABINET.
- *** PHASING PLANS ARE NOT AN EXACT MATCH WITH OVERALL PHASING SEQUENCE. THERE WILL BE OVERLAPPING OF PHASING WORK TO MAINTAIN OPERATION OF EXISTING MCR EQUIPMENT AND CABLING UNTIL NEW EQUIPMENT AND CABLES ARE INSTALLED AND ACTIVE.



1 TECHNOLOGY SITE PLAN
1" = 100'-0"

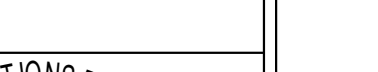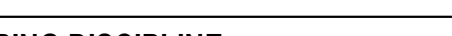		CONSULTANT	ARCHITECT/ENGINEER OF RECORD	STAMP	Office of Construction and Facilities Management	Drawing Title	Phase	Project Title	Project Number		
		ENGINEERING DISCIPLINE:	A/E:			FACILITY SITE PLAN	100% CONSTRUCTION DOCUMENTS	EHRM INFRASTRUCTURE UPGRADES - HAMPTON	509-22-700		
		 www.imegcorp.com 225 W WASHINGTON STREET SUITE 2700 CHICAGO, IL 60606 P: 312.294.0501 F: 312.294.0003 PROJECT #22010109.00	23830 PACIFIC HIGHWAY S. SUITE 203 KENT, WA 98032						 SPEESDESIGNBUILD	Drawing Number	
Revisions:	Date:				Approved:	FULLY SPRINKLERED	Location	Drawing Number			
							HAMPTON VA MEDICAL CENTER, HAMPTON, VIRGINIA	Issue Date	Checked	Drawn	TS-001
								05/09/2025	EW	IMEG	627 of 713

- SHEET NOTES:**
 1. REFER TO SITE PLAN TS001 FOR ADDITIONAL INFORMATION.
 2. REFER TO TS00 AND TS01 FOR CAMPUS OPTICAL FIBER CABLE RISER DIAGRAMS.
 3. REFER TO 27400 FOR HANDHOLE DETAIL.
 4. NEW BACKBONE OPTICAL FIBER CABLES SHALL BE INDOOR/OUTDOOR TYPE.
 5. ALL BACKBONE OPTICAL FIBER CABLE PATHWAYS SHALL BE NEW. DO NOT RE-USE EXISTING BACKBONE CABLE PATHWAYS FOR NEW BACKBONE CABLES.
 6. TRANSITION PVC CONDUITS TO GRC IN CRAWL SPACE OR EXPOSED EXTERIOR LOCATIONS. TRANSITION TO EMT CONDUITS AT INTERIOR OF BUILDING. SEAL ALL PENETRATIONS TO MAINTAIN FIRE-RATINGS OF WALL, CEILING AND FLOORS.
- KEY NOTES: (#)**
 1. PROVIDE PULLBOX ON EXTERIOR WALL AT HEIGHT OF FIRST FLOOR CEILING. ROUTE CONDUIT FROM HANDHOLE UP WALL INTO PULLBOX. PROVIDE PENETRATION THRU WALL AND CONTINUE CONDUIT ROUTE OVER TO TR #5A-7.
 2. PROVIDE A CONDUIT SLEEVE THROUGH THE WALL TO THE CABLE TRAY.

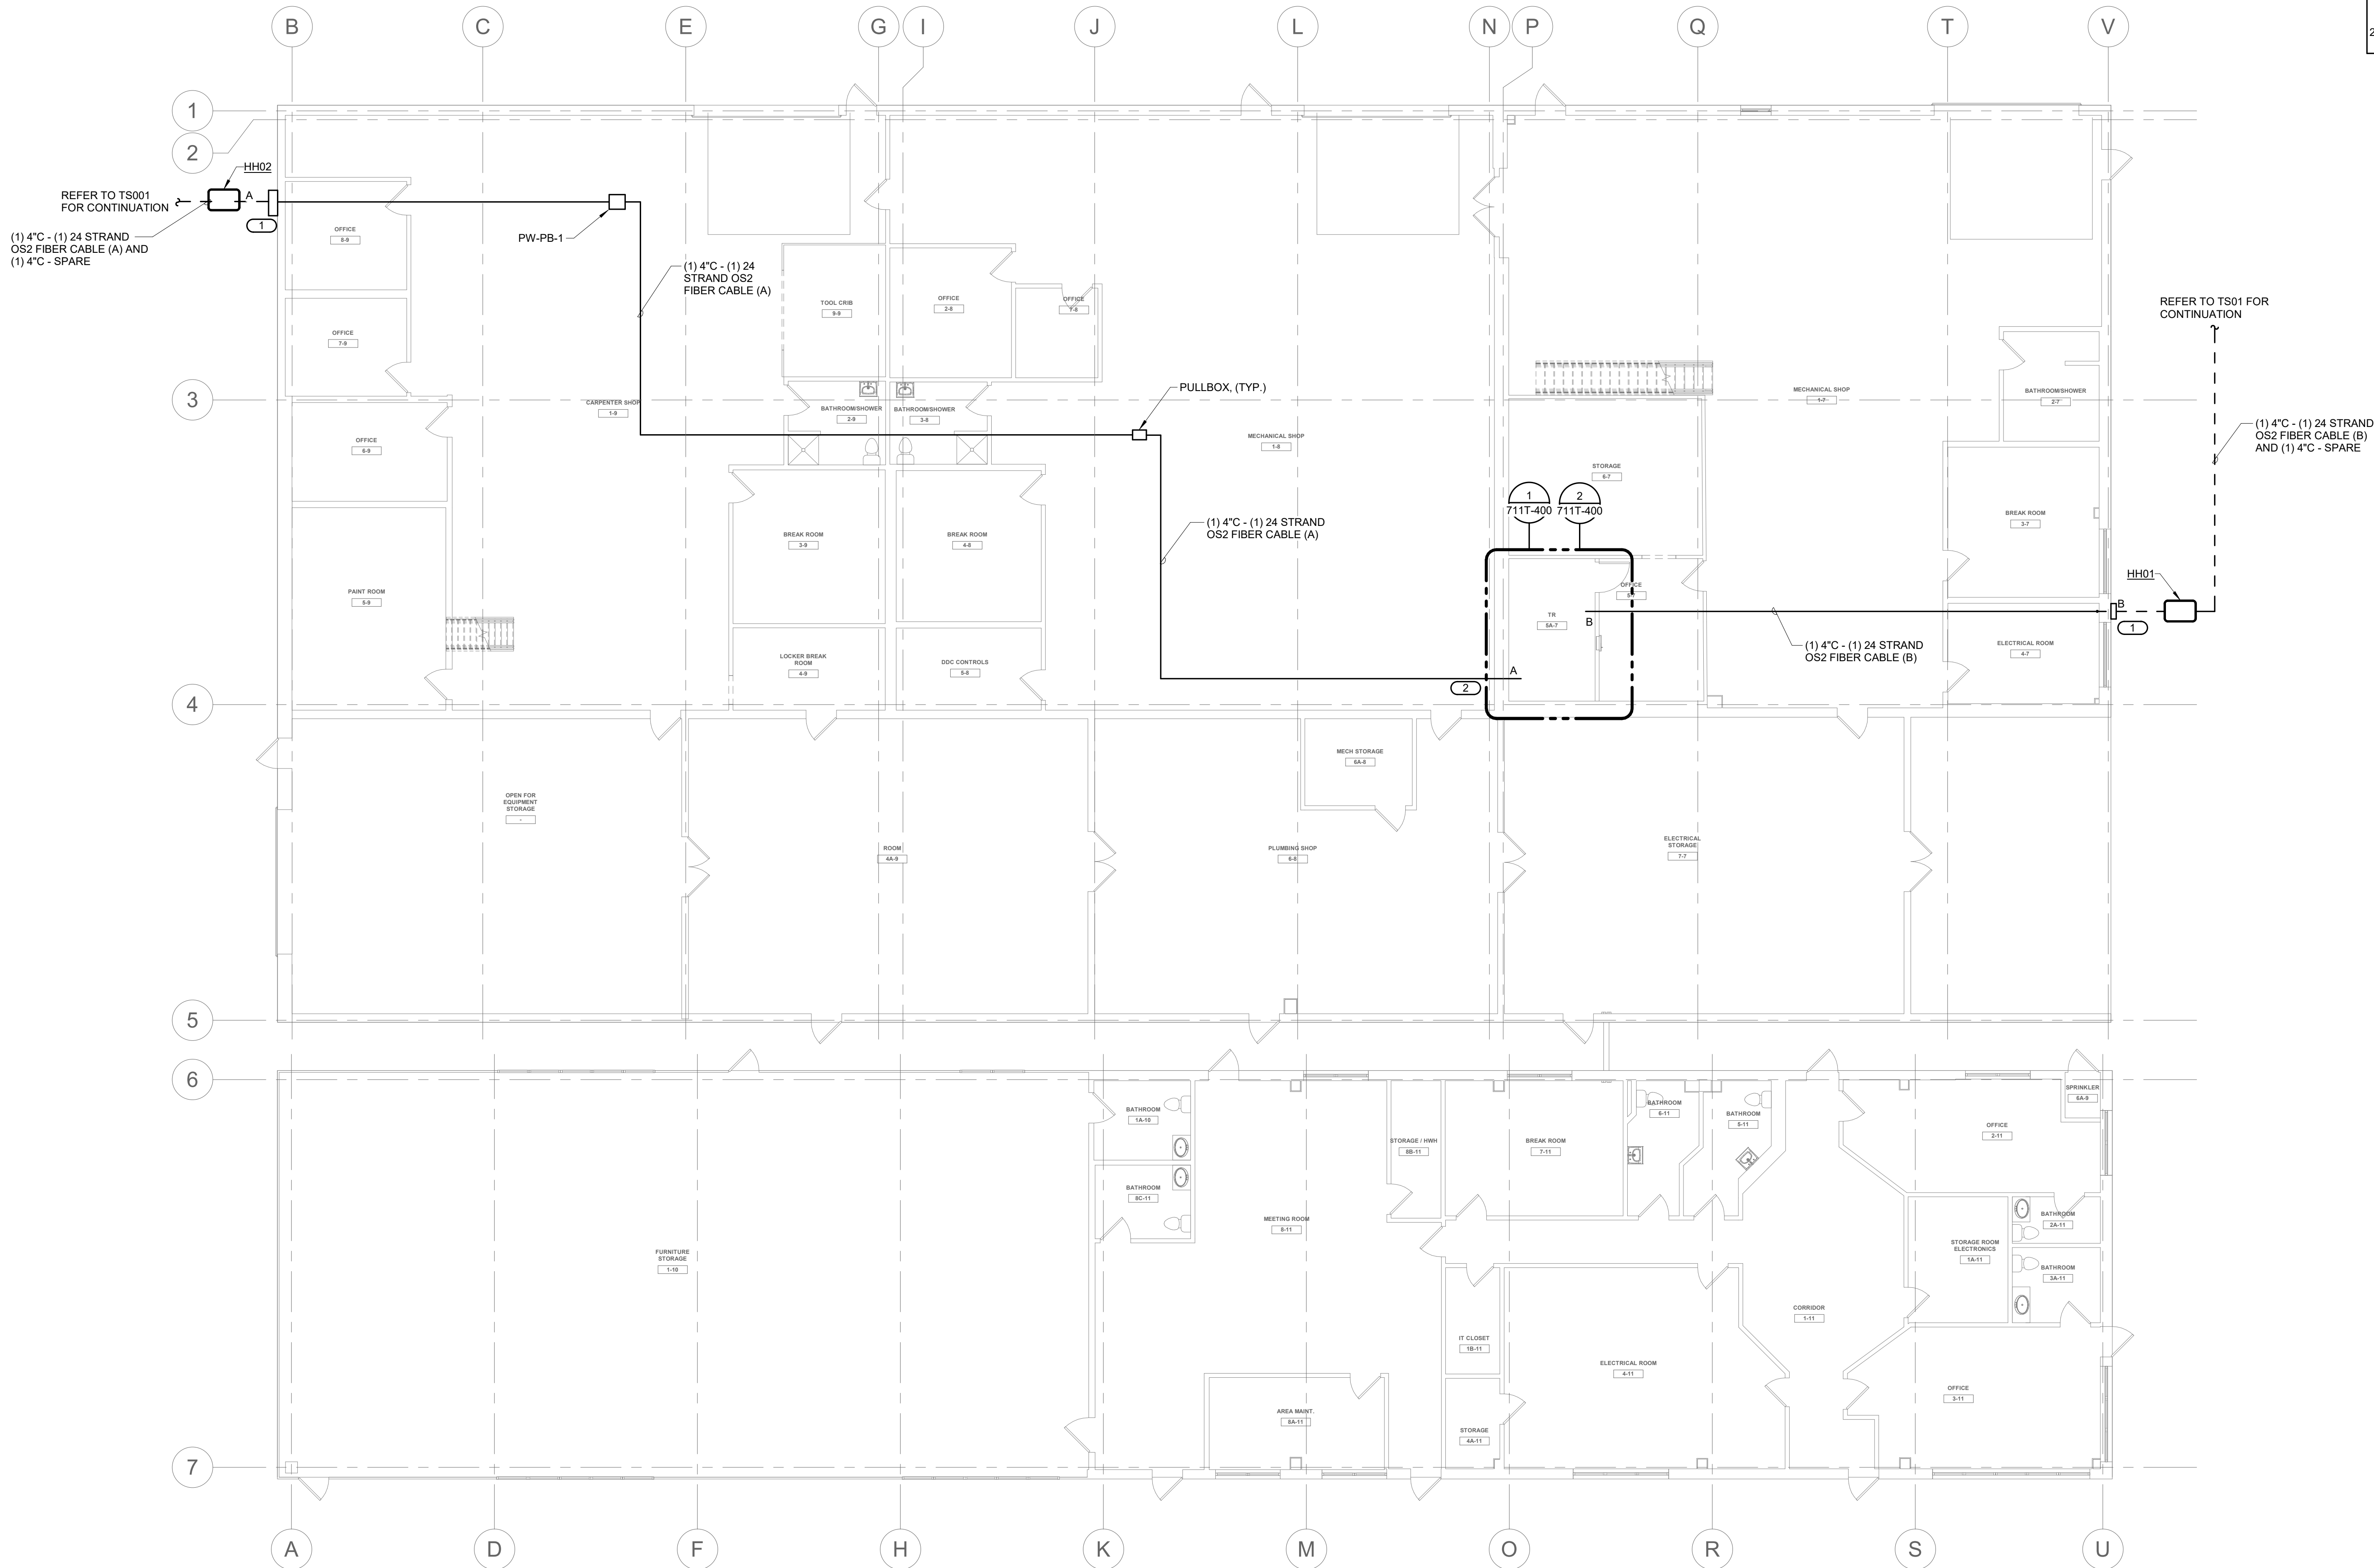

1 LEVEL 01 PLAN - TECHNOLOGY
1/8" = 1'-0"
NORTH

	</
--	--	----

BM 360/509-22-700
VA Hampton EHRM 509-700 B07
000 000 010 011 L1x1x1x1x1

8/2/2025 8:11:27 AM

VA FORM 08 - 6231

Revisions:	Date:

CONSULTANT
ENGINEERING DISCIPLINE:

225 W WASHINGTON STREET SUITE 2700 CHICAGO, IL 60606 P: 312.294.0501 F: 312.294.0003 PROJECT #22010109.00

ARCHITECT/ENGINEER OF RECORD
A/E:
SPEES DESIGN BUILD 23830 PACIFIC HIGHWAY S. SUITE 203 KENT, WA 98032
 SPEESDESIGNBUILD

STAMP


Office of Construction and Facilities Management
 U.S. Department of Veterans Affairs

Drawing Title
BLDG. 07.11 TECHNOLOGY DETAILS AND DIAGRAMS
Approved:

Phase
100% CONSTRUCTION DOCUMENTS
FULLY SPRINKLERED

Project Title
EHRM INFRASTRUCTURE UPGRADES - HAMPTON
Location
HAMPTON VA MEDICAL CENTER, HAMPTON, VIRGINIA
Issue Date
05/09/2025
Checked
EW
Drawn
IMEG

Project Number
509-22-700
Building Number
007-011
Drawing Number
711T-400
629 of 713

A

B

C


D

E

F

- SHEET NOTES:**
1. REFER TO SITEPLAN TS001 FOR ADDITIONAL INFORMATION.
 2. REFER TO TS00 AND TS01 FOR CAMPUS OPTICAL FIBER CABLE RISER DIAGRAMS.
 3. REFER TO 27400 FOR HANDHOLE DETAIL.
 4. NEW BACKBONE OPTICAL FIBER CABLES SHALL BE INDOOR/OUTDOOR TYPE.
 5. ALL BACKBONE OPTICAL FIBER CABLE PATHWAYS SHALL BE NEW. DO NOT RE-USE EXISTING BACKBONE CABLE PATHWAYS FOR NEW BACKBONE CABLES.
 6. TRANSITION PVC CONDUITS TO GRC IN CRAWL SPACE OR EXPOSED EXTERIOR LOCATIONS. TRANSITION TO EMT CONDUITS AT INTERIOR OF BUILDING. SEAL ALL PENETRATIONS TO MAINTAIN FIRE-RATINGS OF WALL, CEILING AND FLOORS.


- KEY NOTES:** (C #)
1. PROVIDE PULLBOX ON EXTERIOR WALL AT HEIGHT ABOVE FINISHED CEILING. ROUTE CONDUIT UP WALL INTO PULLBOX. PROVIDE PENETRATION THRU WALL AND ROUTE CORE A CONDUIT THRU WALL ABOVE FINISHED CEILING AND INTO TR #A51.
 2. ROUTE CONDUIT WITH CORE A FIBER FOR BLDG #14 ABOVE CEILING TO COMMON WALL BETWEEN BLDGS. PROVIDE PENETRATION THRU WALL AND ROUTE CONDUIT INTO BLDG #14 ABOVE CEILING AND OVER TO TR#A2A. REFER TO BLDG 14 PLANS FOR ADDITIONAL WORK REQUIREMENTS.
 3. PROVIDE PENETRATION THROUGH COMMON WALL AND ROUTE CONDUIT WITH CORE B FIBER INTO BLDG #13 ABOVE CEILING AND OVER TO TR#A51. REFER TO BLDG 14 PLANS FOR ADDITIONAL WORK REQUIREMENTS.

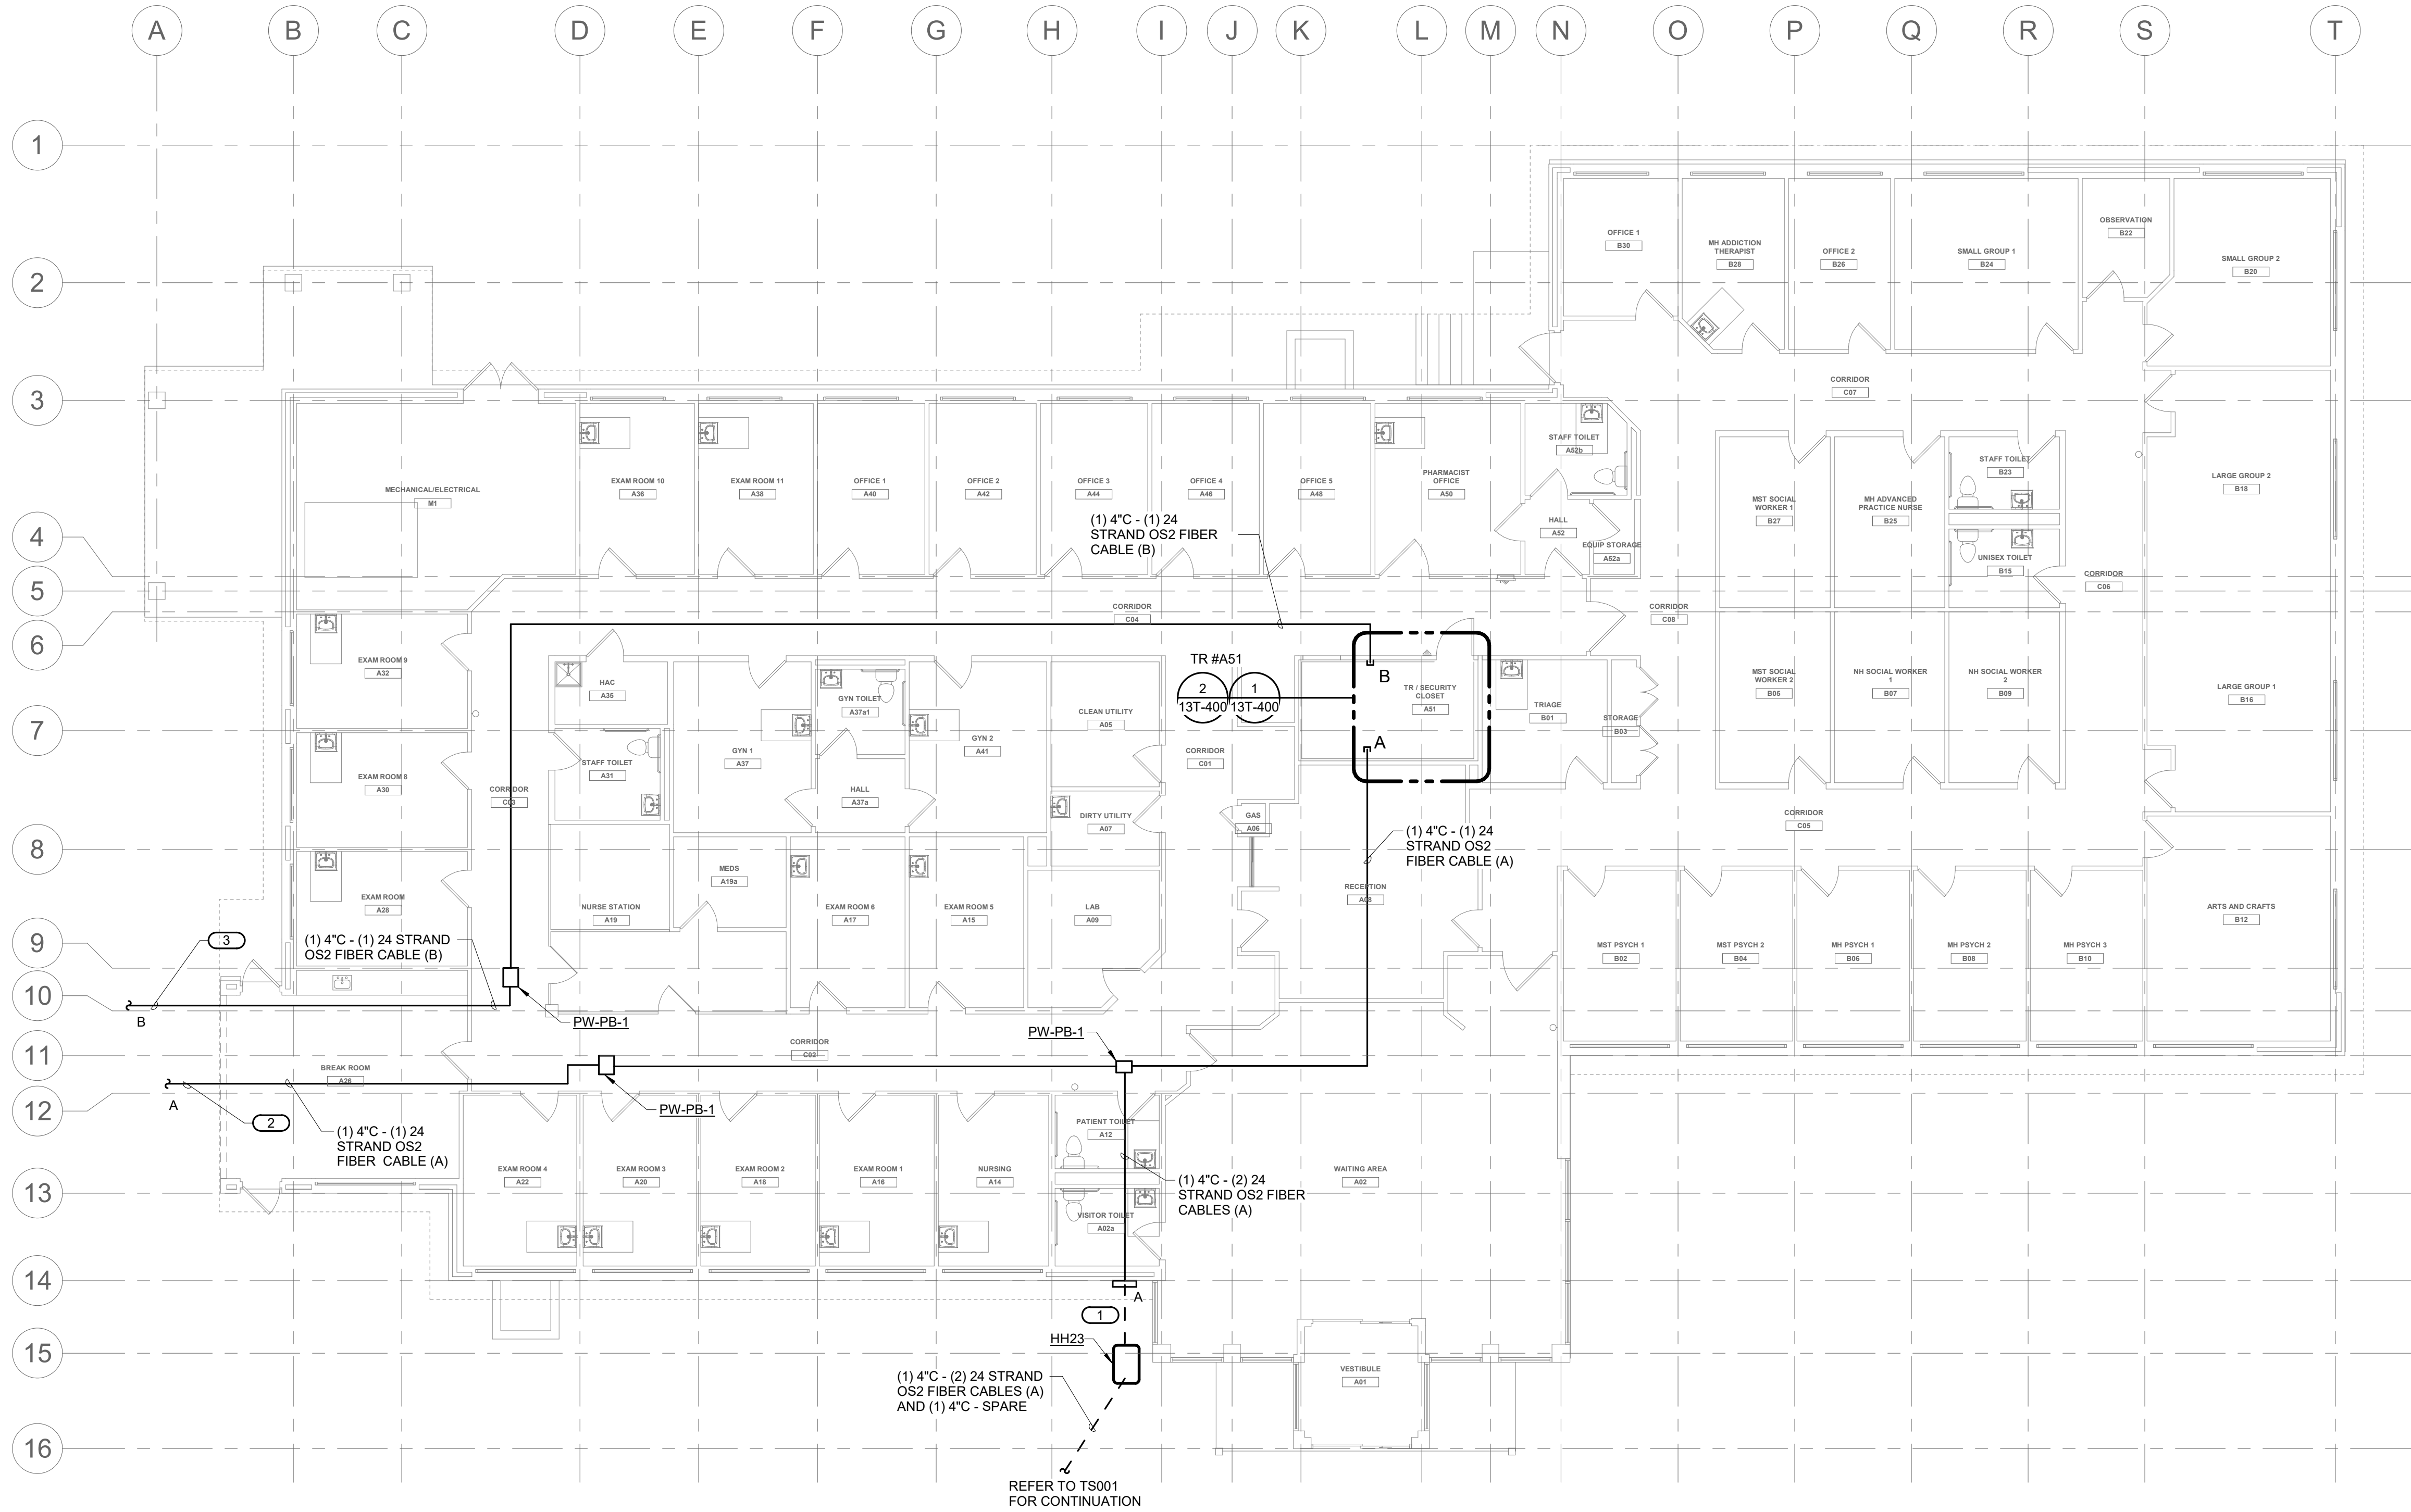

1 LEVEL 01 PLAN - TECHNOLOGY


1/8" = 1'-0"

--	--	

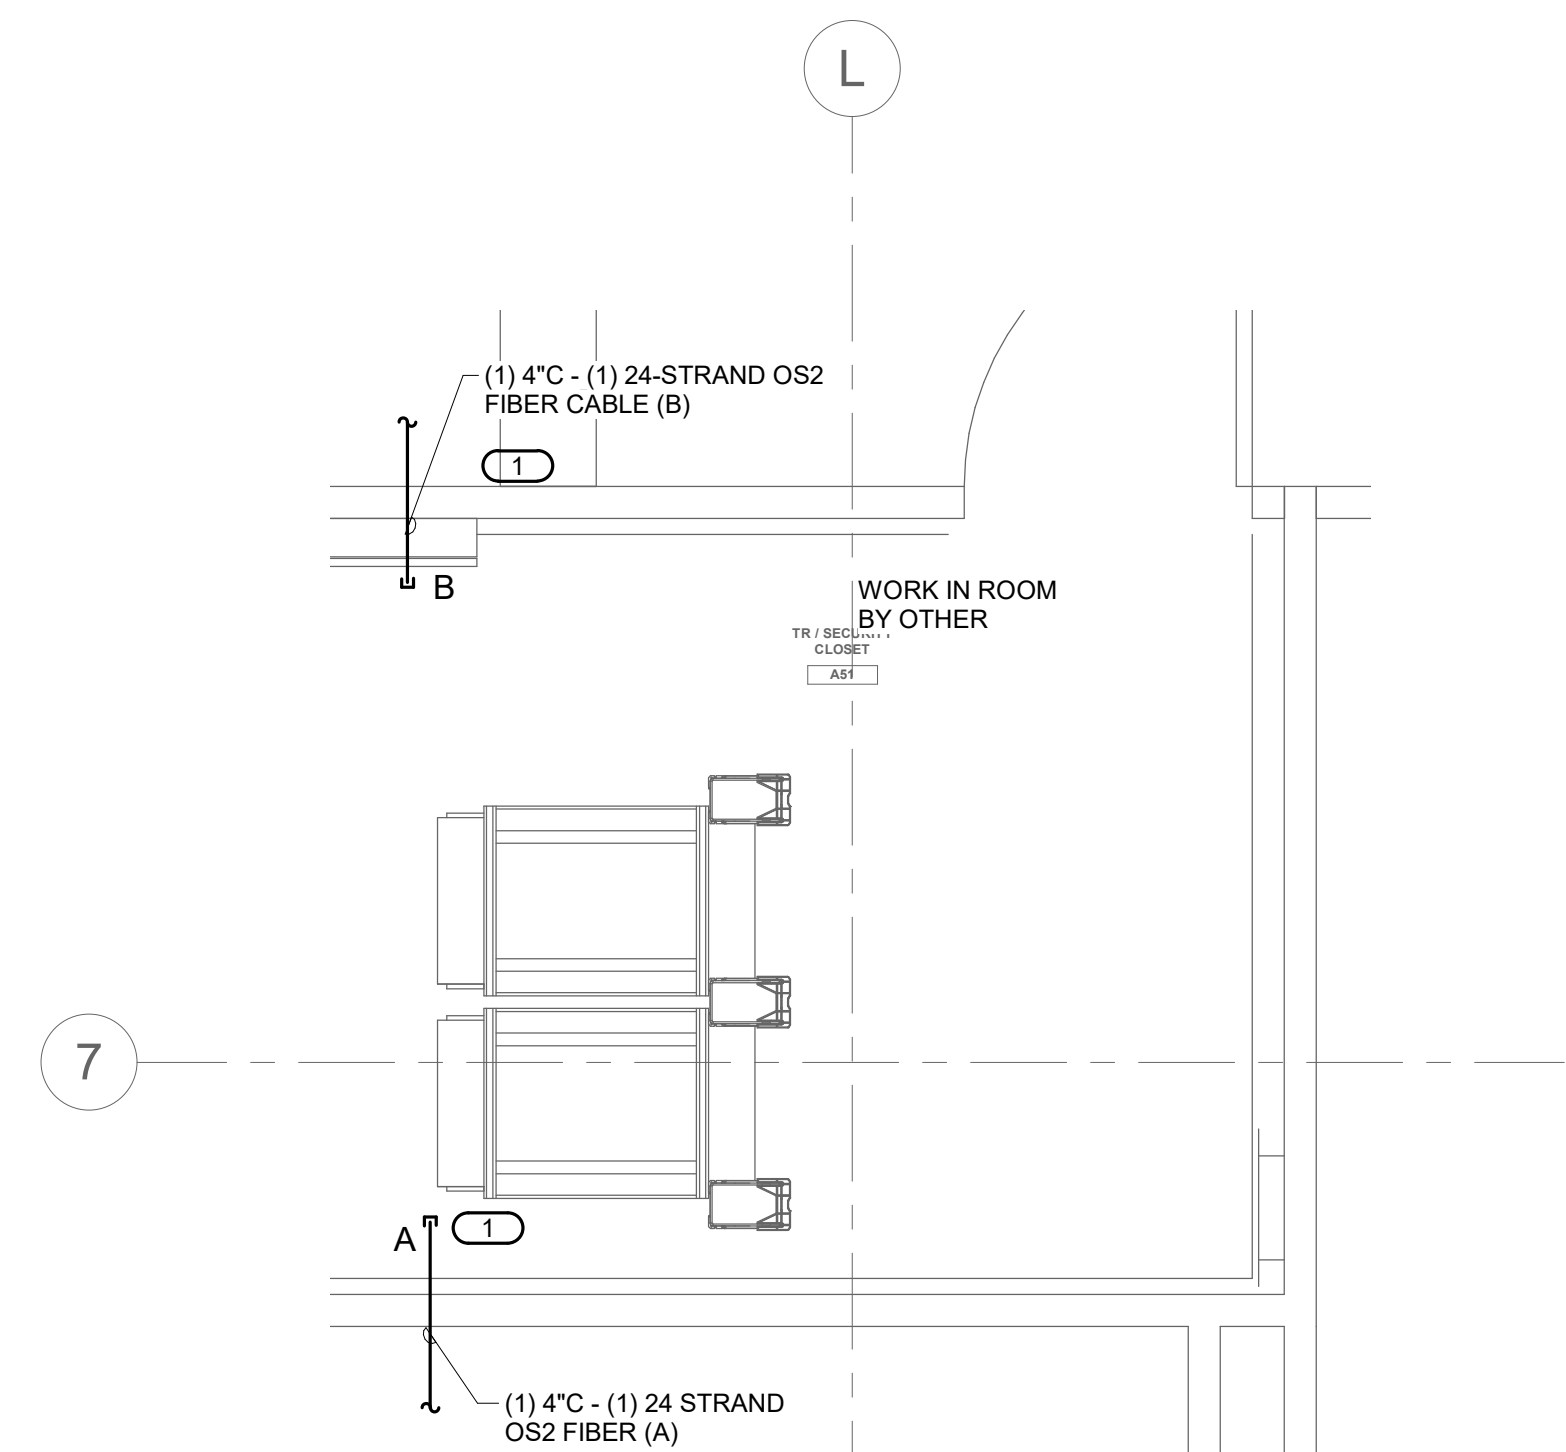

1 TELECOM ROOM ENLARGEMENT TR #A51
1/2" = 1'-0"


- NOTES:
- REFER TO ELECTRICAL DRAWINGS FOR ROOM LAYOUT AND RACK ELEVATIONS.
 - ROUTE OPTICAL FIBER CABLE TO OVERHEAD CABLE TRAY AND TERMINATE IN FIBER DISTRIBUTION CABINET.
- KEY NOTES: C #
- THROUGH WALL PENETRATION FOR BACKBONE CONDUIT. OPTICAL FIBER CABLE CONTINUES ON CABLE TRAY TO RACKS.

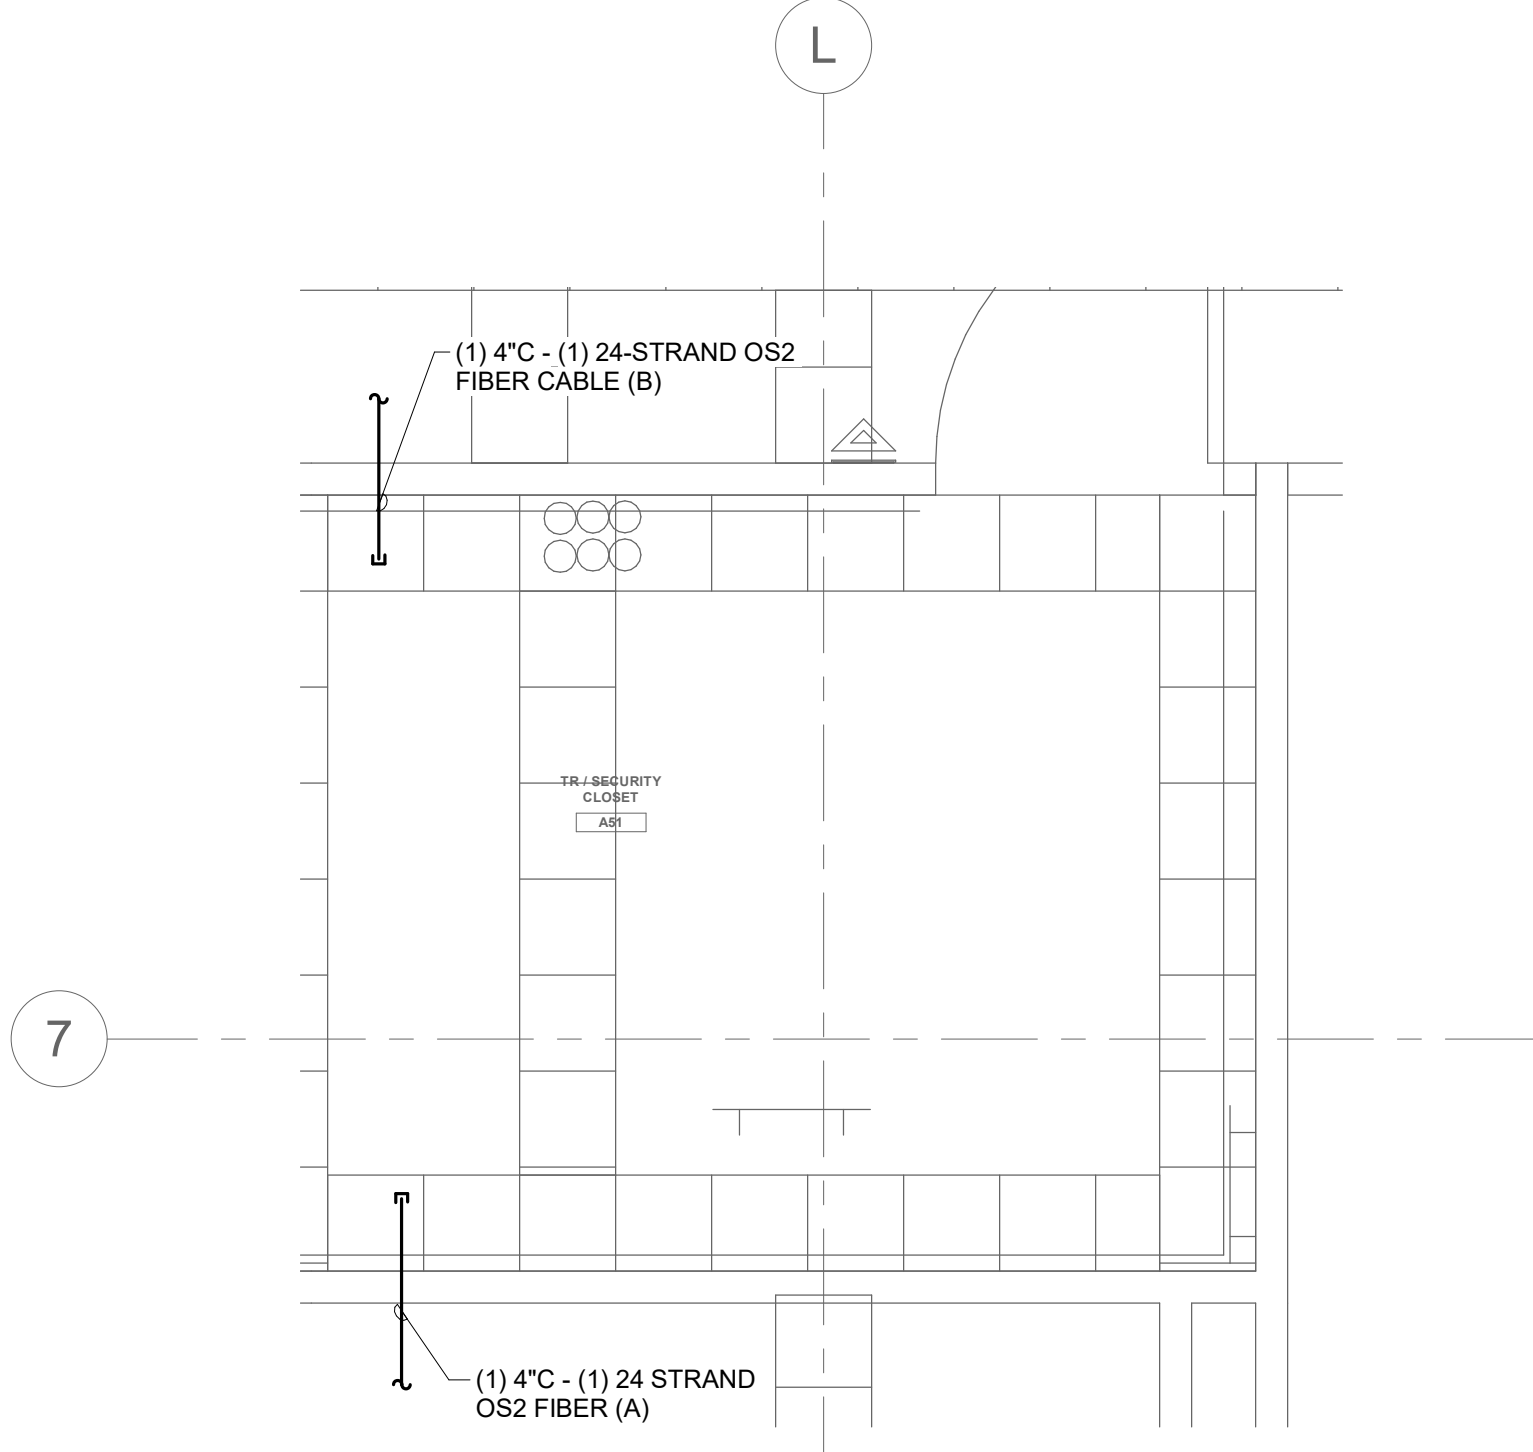

2 TELECOM ROOM PATHWAY TR #A51
1/2" = 1'-0"

3 FIBER RISER DIAGRAM

- NO SCALE
- NOTES:
- THIS RISER IS DIAGRAMMATIC AND MAY NOT SHOW ACTUAL ROUTING OR QUANTITIES OF MATERIALS SHOWN. THIS RISER IS SHOWN FOR CLARIFICATION OF CONNECTION(S), LOCATIONS AND CABLE TYPE. ALL INFORMATION OUTLETS ARE TYPICAL OF THE OUTLETS IN THE AREA SHOWN. REFER TO FLOOR PLANS FOR MORE SPECIFIC ROUTING INFORMATION. REFER TO SPECIFICATIONS FOR ADDITIONAL REQUIREMENTS.
 - REFER TO TECHNOLOGY DRAWINGS FOR CHANNEL RACK AND FIBER OPTIC DISTRIBUTION CABINET SPECIFICATIONS

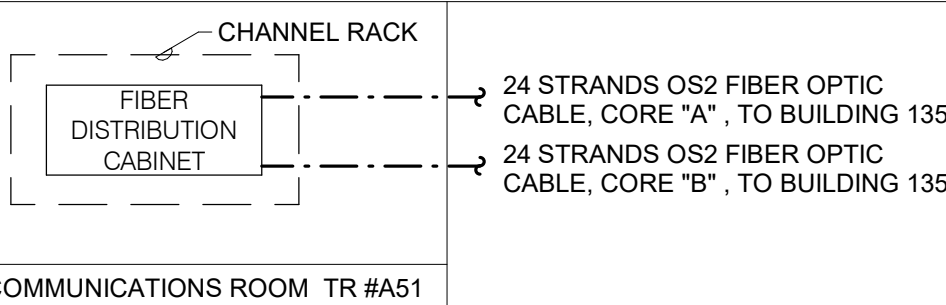

LEVEL 01

CONSULTANT
ENGINEERING DISCIPLINE:
IMEG
www.imegcorp.com
225 W WASHINGTON STREET
SUITE 2700
CHICAGO, IL 60606
P: 312.294.0501 F: 312.294.0003
PROJECT #22010109.00

ARCHITECT/ENGINEER OF RECORD
A/E:
SPEES DESIGN BUILD
23830 PACIFIC HIGHWAY S. SUITE 203
KENT, WA 98032
SDB SPEESDESIGNBUILD

STAMP
REGISTERED COMMUNICATIONS DISTRIBUTION DESIGNER
Bicsi
ES-95-C, WIRE-2
Reg. No. 1579026
EXPIRES 03-31-2025
RCDD
[Signature]

Office of
Construction
and Facilities
Management
VA U.S. Department
of Veterans Affairs

Drawing Title
BLDG. 13 TECHNOLOGY DETAILS AND
DIAGRAMS

Approved:

Phase
100% CONSTRUCTION
DOCUMENTS

FULLY SPRINKLERED

Project Title
EHRM INFRASTRUCTURE
UPGRADES - HAMPTON

Location
HAMPTON VA MEDICAL CENTER, HAMPTON, VIRGINIA

Issue Date
05/09/2025


Checked
EW

Drawn
IMEG

Project Number
509-22-700
Building Number
13

Drawing Number
13T-400
631 of 713

A
B
C
D
E
F

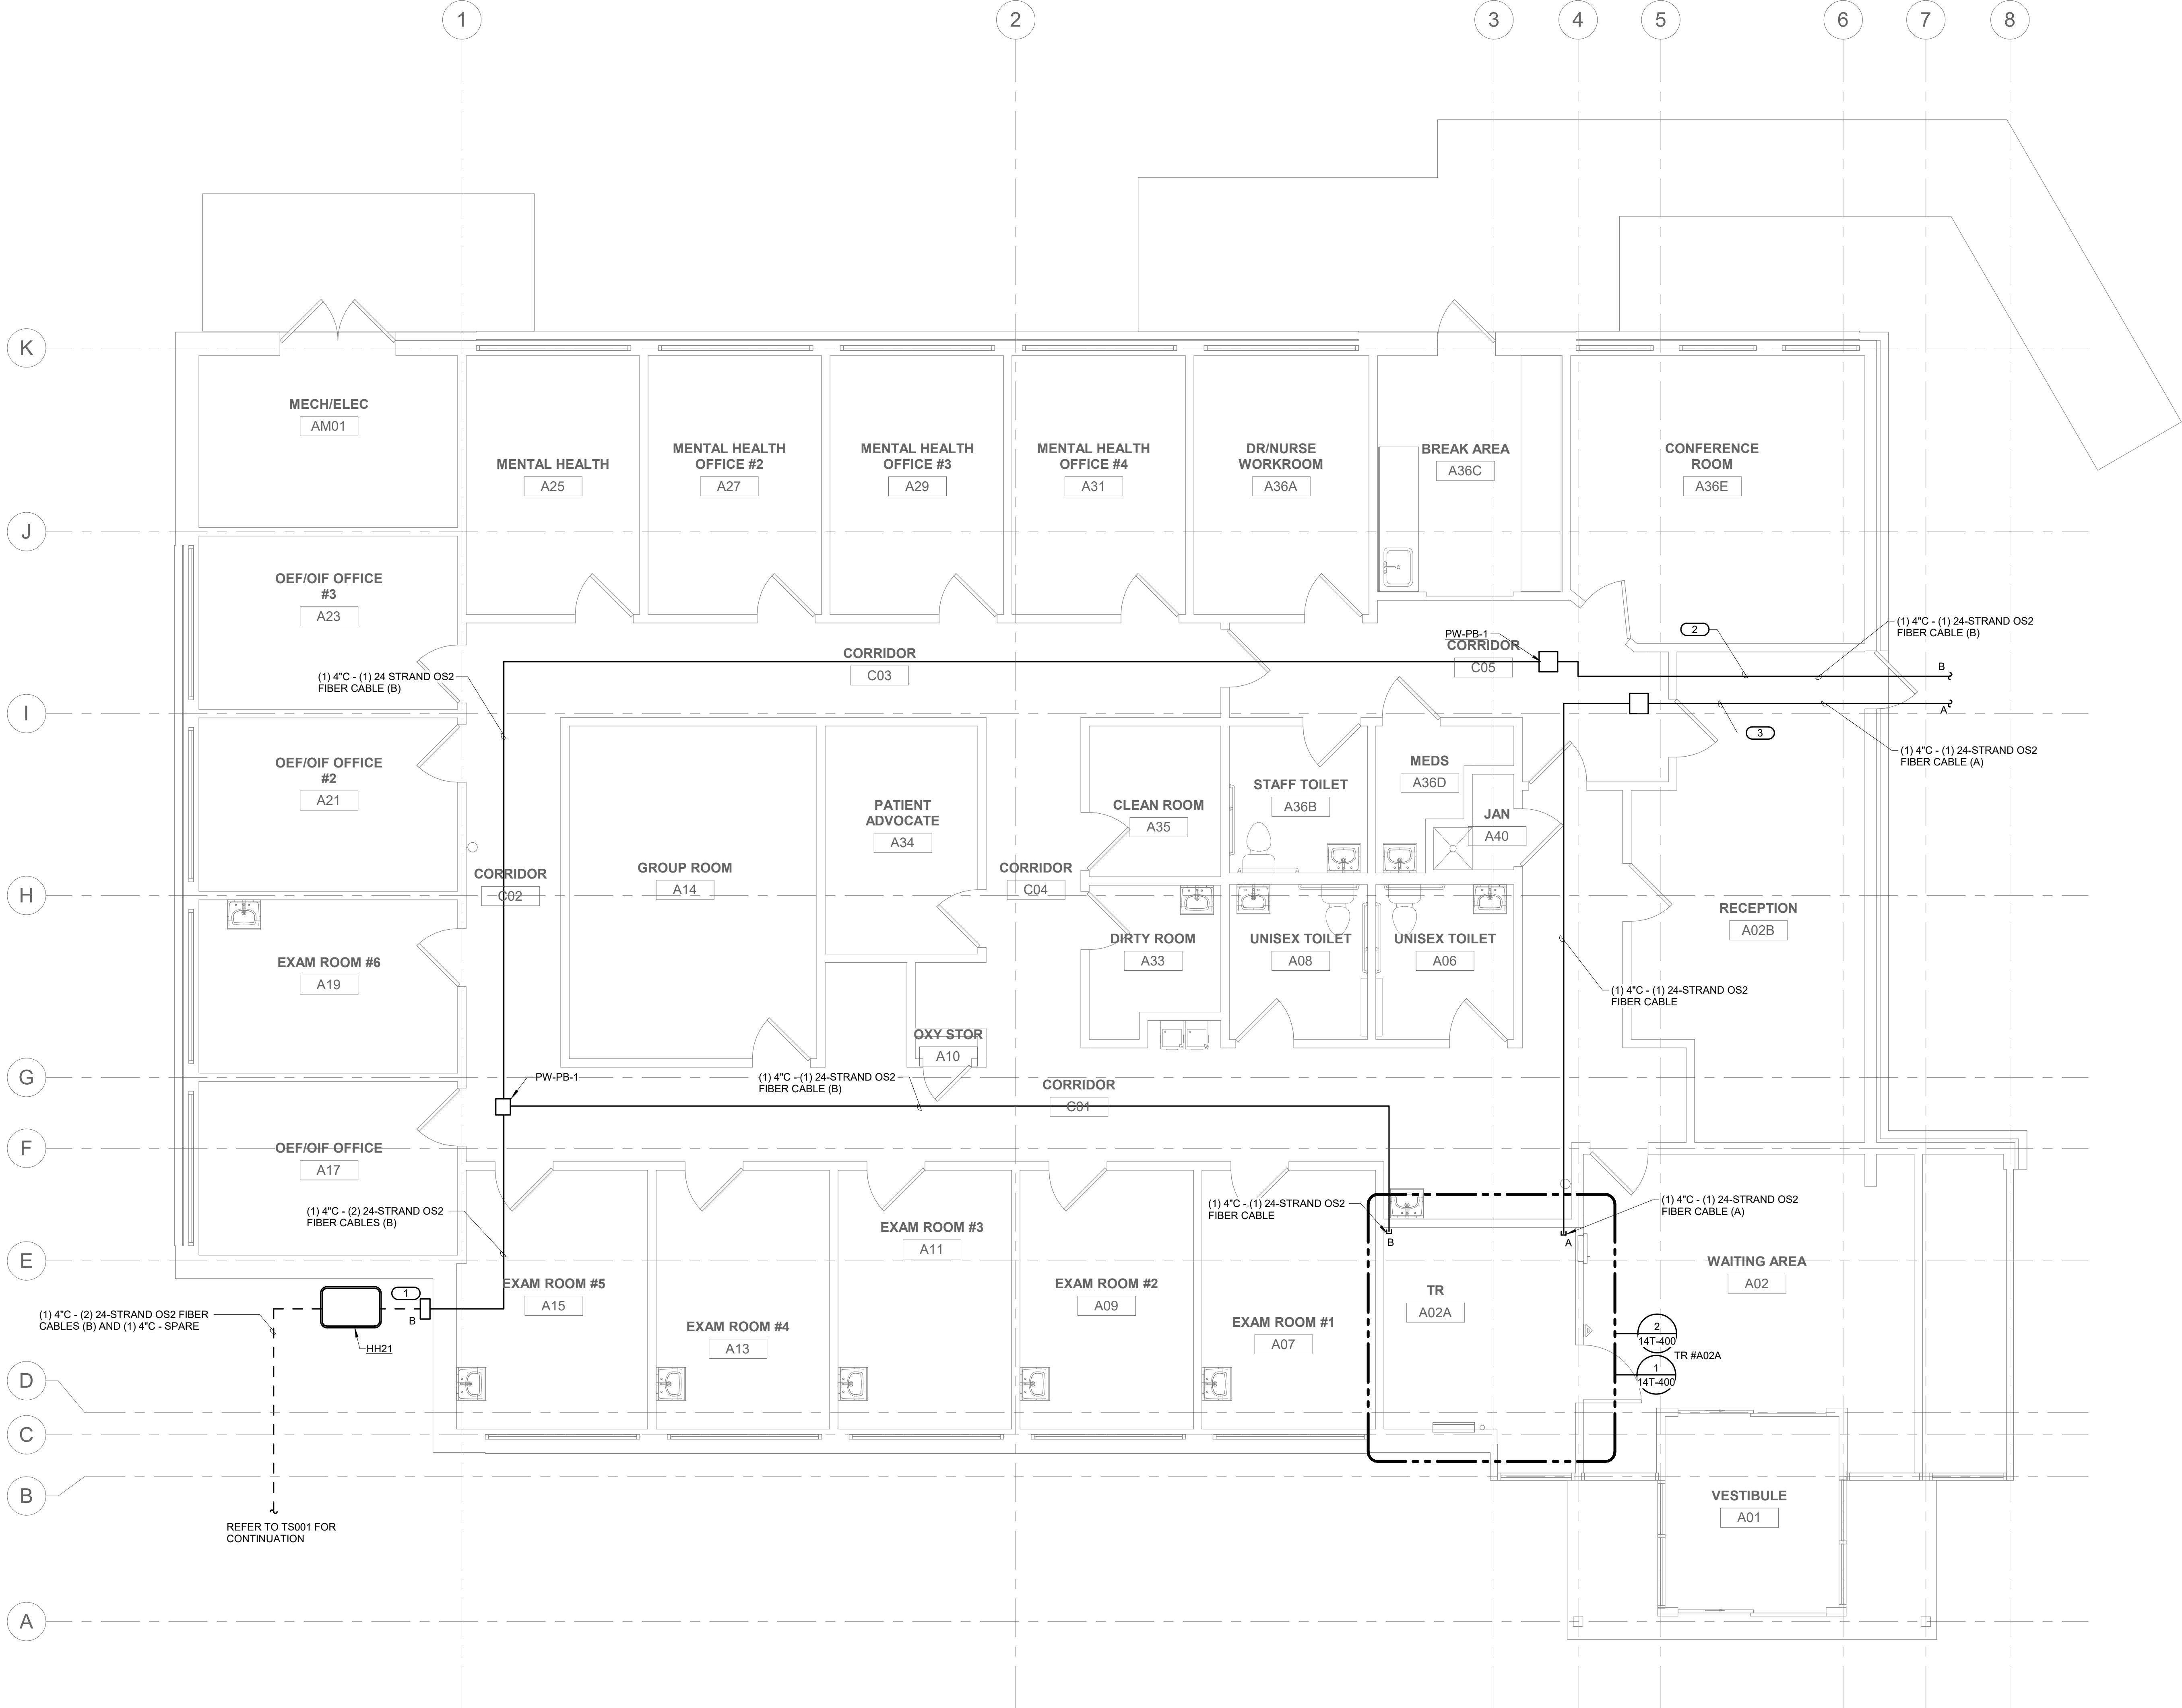

- SHEET NOTES:**
1. REFER TO SITEPLAN TS001 FOR ADDITIONAL INFORMATION.
 2. REFER TO TS00 AND TS01 FOR CAMPUS OPTICAL FIBER CABLE RISER DIAGRAMS.
 3. REFER TO 27400 FOR HANDHOLE DETAIL.
 4. NEW BACKBONE OPTICAL FIBER CABLES SHALL BE INDOOR/OUTDOOR TYPE.
 5. ALL BACKBONE OPTICAL FIBER CABLE PATHWAYS SHALL BE NEW. DO NOT RE-USE EXISTING BACKBONE CABLE PATHWAYS FOR NEW BACKBONE CABLES.
 6. TRANSITION PVC CONDUITS TO GRC IN CRAWL SPACE OR EXPOSED EXTERIOR LOCATIONS. TRANSITION TO EMT CONDUITS AT INTERIOR OF BUILDING. SEAL ALL PENETRATIONS TO MAINTAIN FIRE-RATINGS OF WALL, CEILING AND FLOORS.
- KEY NOTES: (#)**
1. PROVIDE PULLBOX ON EXTERIOR WALL AT HEIGHT ABOVE FINISHED CEILING. ROUTE CONDUIT UP WALL INTO PULLBOX. PROVIDE PENETRATION THRU WALL AND ROUTE CORE B CONDUIT THROUGH WALL ABOVE FINISHED CEILING AND INTO TR #A02A.
 2. ROUTE CONDUIT WITH CORE B FIBER FOR BLDG #14 ABOVE CEILING TO COMMON WALL BETWEEN BLDGS. PROVIDE PENETRATION THRU WALL AND ROUTE CONDUIT INTO BLDG #14 ABOVE CEILING AND OVER TO TR#A02A. REFER TO BLDG 14 PLANS FOR ADDITIONAL WORK REQUIREMENTS.
 3. PROVIDE PENETRATION THROUGH COMMON WALL AND ROUTE CONDUIT WITH CORE A FIBER INTO BLDG #13 ABOVE CEILING AND OVER TO TR#A51. REFER TO BLDG 14 PLANS FOR ADDITIONAL WORK REQUIREMENTS.

1 LEVEL 01 PLAN - TECHNOLOGY
1/4" = 1'-0"

B:\A\360\509-22-700
HAMPTON
E:\A\360-700\B14.T_R1.rvt
8/13/2025 11:57:49 AM

Revisions:	Date:	CONSULTANT ENGINEERING DISCIPLINE: IMEG www.imegcorp.com 225 W WASHINGTON STREET SUITE 2700 CHICAGO, IL 60606 P: 312.294.0501 F: 312.294.0003 PROJECT #22010109.00	ARCHITECT/ENGINEER OF RECORD A/E: SDB SPEEDSDSIGNBUILD 23830 PACIFIC HIGHWAY S. SUITE 203 KENT, WA 98032	STAMP Bicsi EDWIN C. BICSI, JR. Reg. No. 1519026 EXPIRES 12-31-2025 RCDD	Office of Construction and Facilities Management VA U.S. Department of Veterans Affairs	Drawing Title BLDG.14 LEVEL 01 PLAN - TECHNOLOGY	Phase 100% CONSTRUCTION DOCUMENTS	Project Title EHRM INFRASTRUCTURE UPGRADES - HAMPTON	Project Number 509-22-700	
								Building Number 14		
						Approved:	FULLY SPRINKLERED	Location HAMPTON VA MEDICAL CENTER, HAMPTON, VIRGINIA	Drawing Number 14T-201	
								Issue Date 05/09/2025	Checked EW	Drawn IMEG

BM 360/509-22-700
VA Hampton
EHRM 509-700 BLDG 14 T_021.rvt

8/13/2025 11:57:50 AM

VA FORM 08 - 6231

Revisions:	
Date:	

CONSULTANT

ENGINEERING DISCIPLINE:


www.imegcorp.com
225 W WASHINGTON STREET
SUITE 2700
CHICAGO, IL 60606
P: 312.294.0501 F: 312.294.0003
PROJECT #22010109.00

ARCHITECT/ENGINEER OF RECORD

A/E:

SPEES DESIGN BUILD
23830 PACIFIC HIGHWAY S. SUITE 203
KENT, WA 98032

 SPEESDESIGNBUILD

STAMP



Office of
Construction
and Facilities
Management

 U.S. Department
of Veterans Affairs

Drawing Title

BLDG.14 TECHNOLOGY DETAILS AND
DIAGRAMS

Approved:

Phase

100% CONSTRUCTION
DOCUMENTS

FULLY SPRINKLERED

Project Title

EHRM INFRASTRUCTURE
UPGRADES - HAMPTON

Location

HAMPTON VA MEDICAL CENTER, HAMPTON, VIRGINIA

Issue Date

05/09/2025

Checked

EW

Drawn

IMEG

Project Number

509-22-700

Building Number

14

Drawing Number

14T-400

633 of 713

A

B

C

D

E


F

SHEET NOTES:

1. REFER TO SITEPLAN T5001 FOR ADDITIONAL INFORMATION.
2. REFER TO T500 AND T501 FOR CAMPUS OPTICAL FIBER CABLE SYSTEM DIAGRAMS.
3. REFER TO T2400 FOR HANDHOLE DETAIL.
4. NEW BACKBONE OPTICAL FIBER CABLES SHALL BE INDOOR/OUTDOOR TYPE.
5. ALL BACKBONE OPTICAL FIBER CABLE PATHWAYS SHALL BE NEW AND NOT RE-USE EXISTING BACKBONE CABLE PATHWAYS FOR NEW BACKBONE CABLES.
6. TRANSITION PVC CONDUITS TO GRC IN CRAWL SPACE OR EXPOSED EXTERIOR LOCATIONS. TRANSITION TO EMT CONDUIT IN INTERIOR OF BUILDING. SEAL ALL PENETRATIONS TO MAINTAIN FIRE-RATINGS OF WALL, CEILING AND FLOORS.

KEY NOTES: #

1. PROVIDE PULLBOX ON EXTERIOR WALL AT HEIGHT OF FIRST FLOOR CEILING. ROUTE CONDUITS UP ALONG WALL TO PULLBOX. PROVIDE PENETRATIONS THRU WALL. ROUTE CONDUITS THRU PULLBOX INTO BLDG 15.
2. CONTINUE ROUTE OF CONDUITS UP TO FIRST FLOOR CEILING DECK. PROVIDE PENETRATION THRU CEILING AND ROUTE CONDUITS UP INTO SECOND FLOOR.

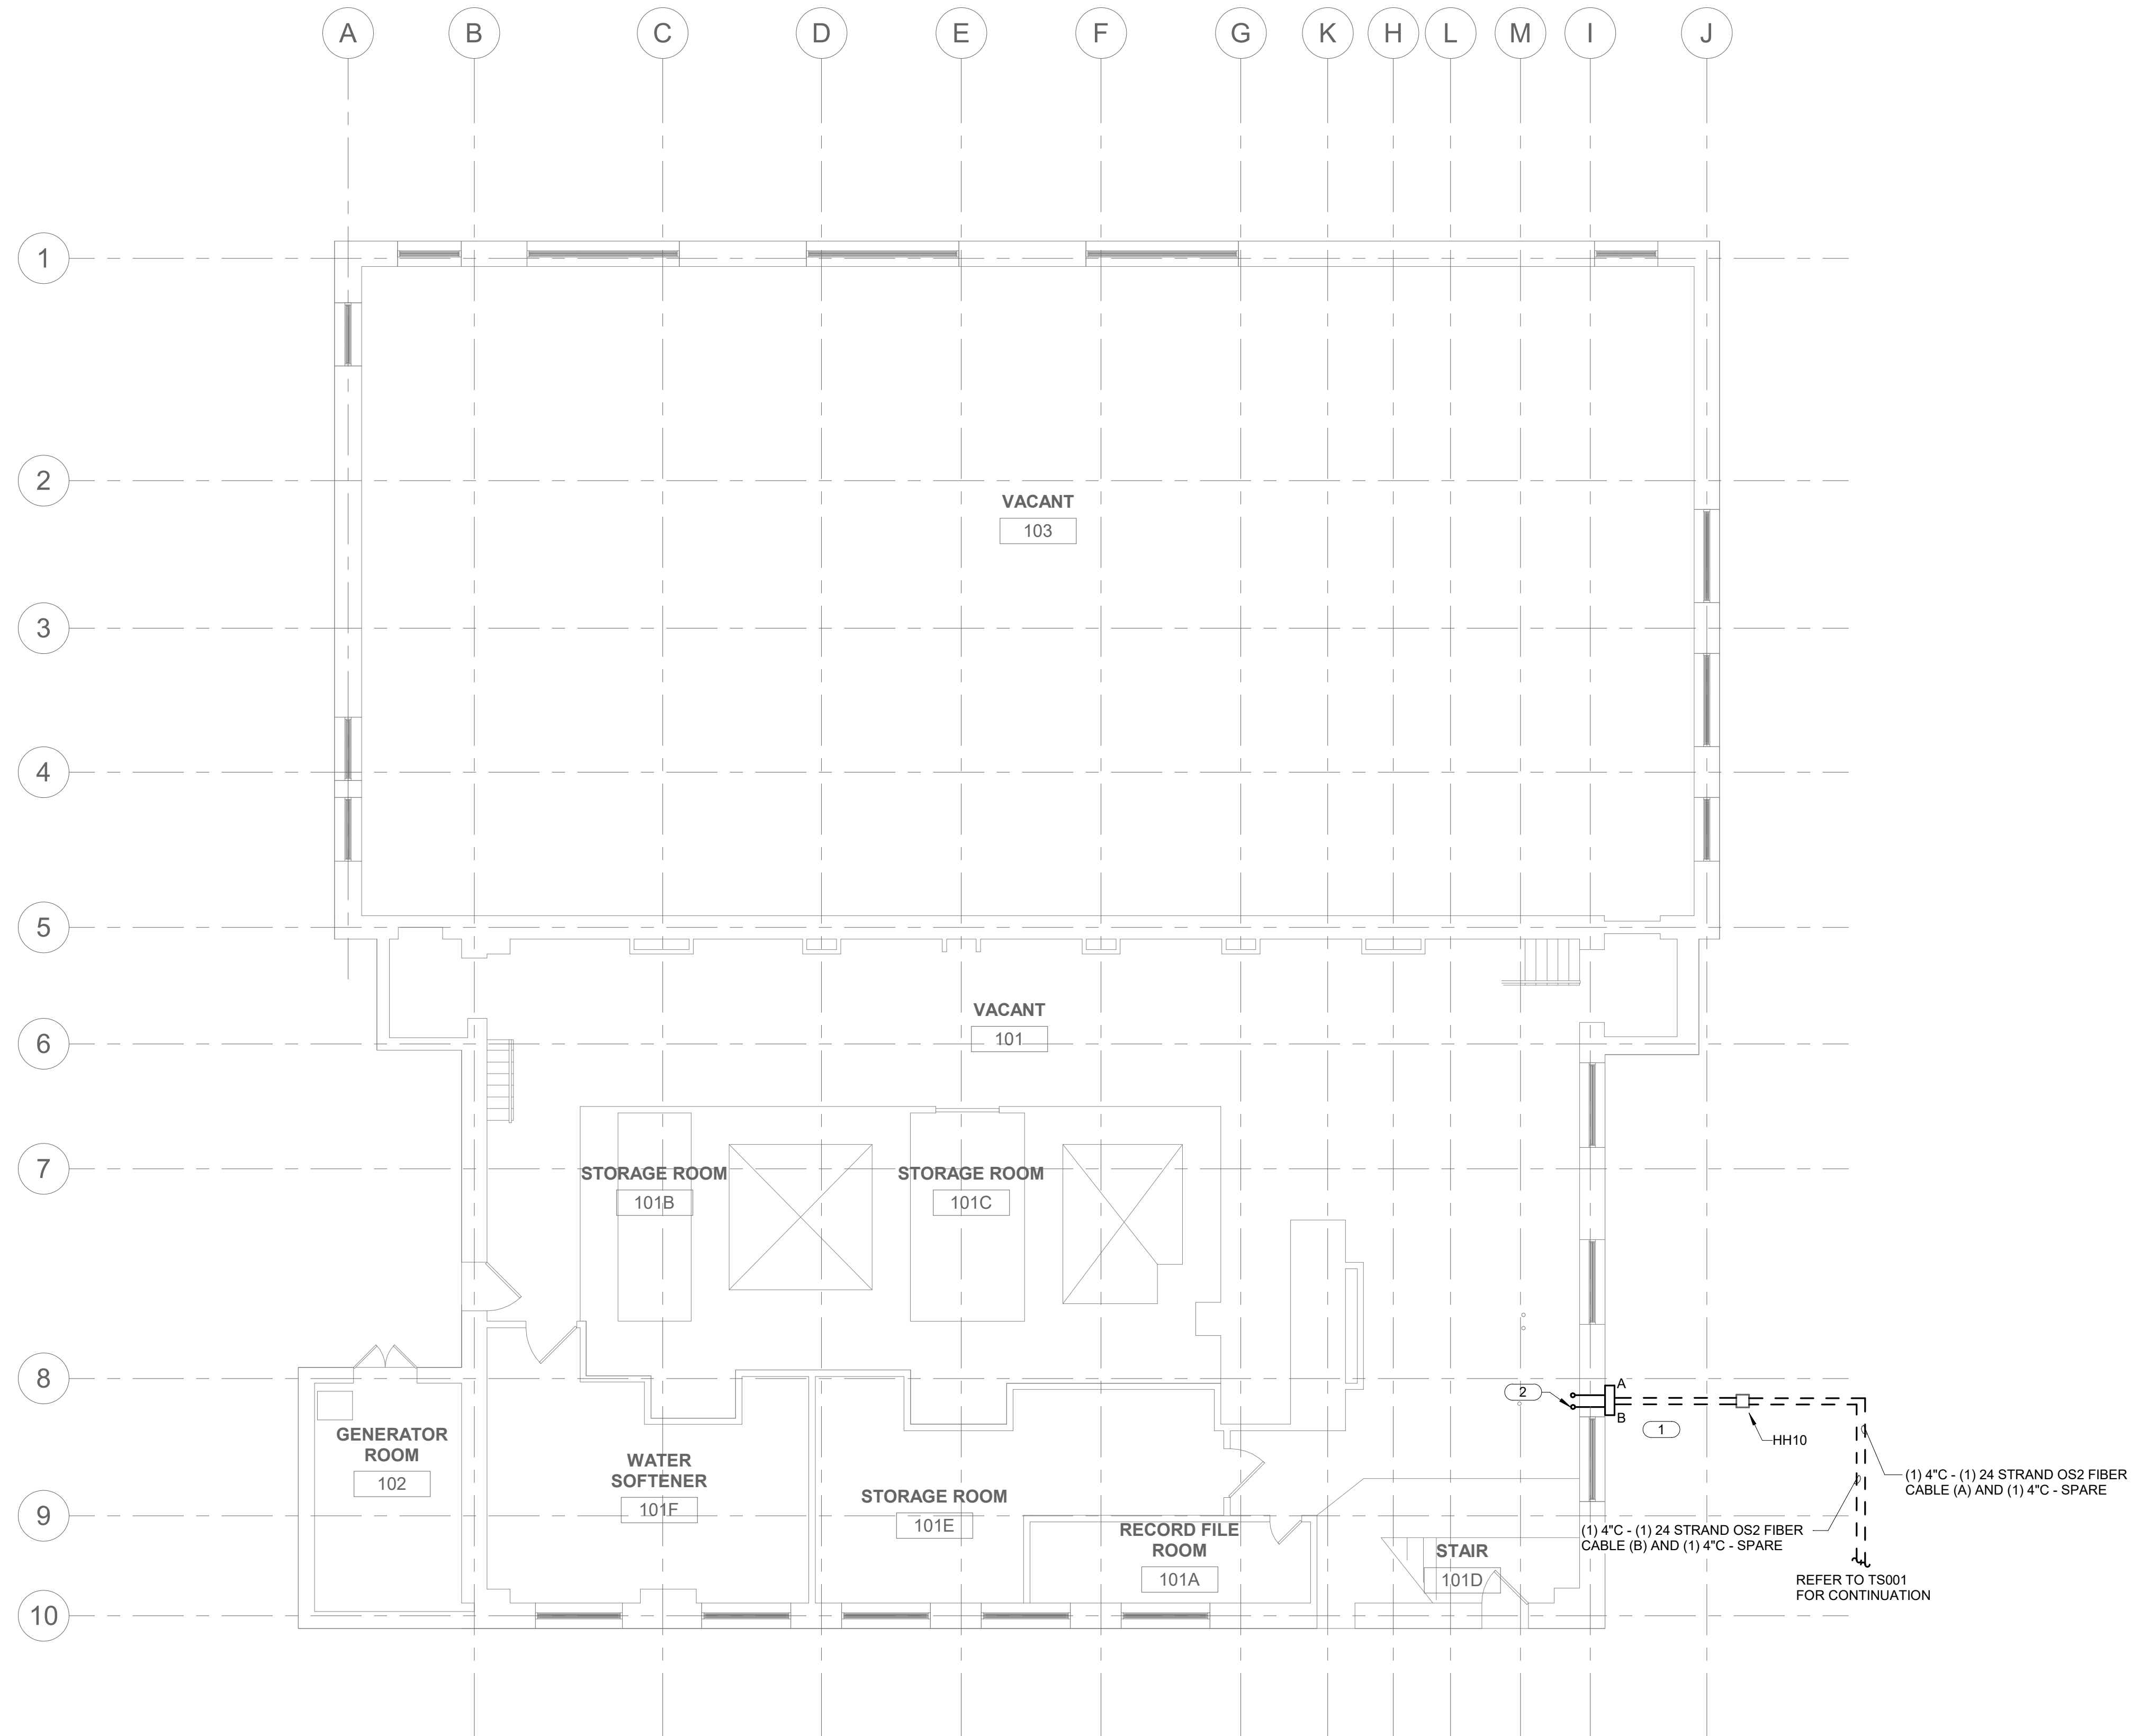

1 LEVEL 01 PLAN - TECHNOLOGY

[illegible]

- SHEET NOTES:
1. REFER TO SITEPLAN TS001 FOR ADDITIONAL INFORMATION.

2. REFER TO TS00 AND TS01 FOR CAMPUS OPTICAL FIBER CABLE RISER DIAGRAMS.


3. REFER TO 2/T400 FOR HANDHOLE DETAIL.

4. NEW BACKBONE OPTICAL FIBER CABLES SHALL BE INDOOR/OUTDOOR TYPE.

5. ALL BACKBONE OPTICAL FIBER CABLE PATHWAYS SHALL BE NEW. DO NOT RE-USE EXISTING BACKBONE CABLE PATHWAYS FOR NEW BACKBONE CABLES.

6. TRANSITION PVC CONDUITS TO GRC IN CRAWL SPACE OR EXPOSED EXTERIOR LOCATIONS. TRANSITION TO EMT CONDUITS AT INTERIOR OF BUILDING. SEAL ALL PENETRATIONS TO MAINTAIN FIRE-RATINGS OF WALL, CEILING AND FLOORS.
- KEY NOTES: C #
1. PROVIDE FURRED-OUT WALL PARTITION TO CONCEAL CONDUIT FOR ROUTE THRU ROOM #302. CONTINUE ROUTE OF CONDUITS UP TO CEILING AND OVER TO LOCATION BELOW TR #302A AT CATWALK.


2. PROVIDE PENETRATIONS THRU CEILING DECK AND ROUTE CONDUITS UP INTO TR #302A.

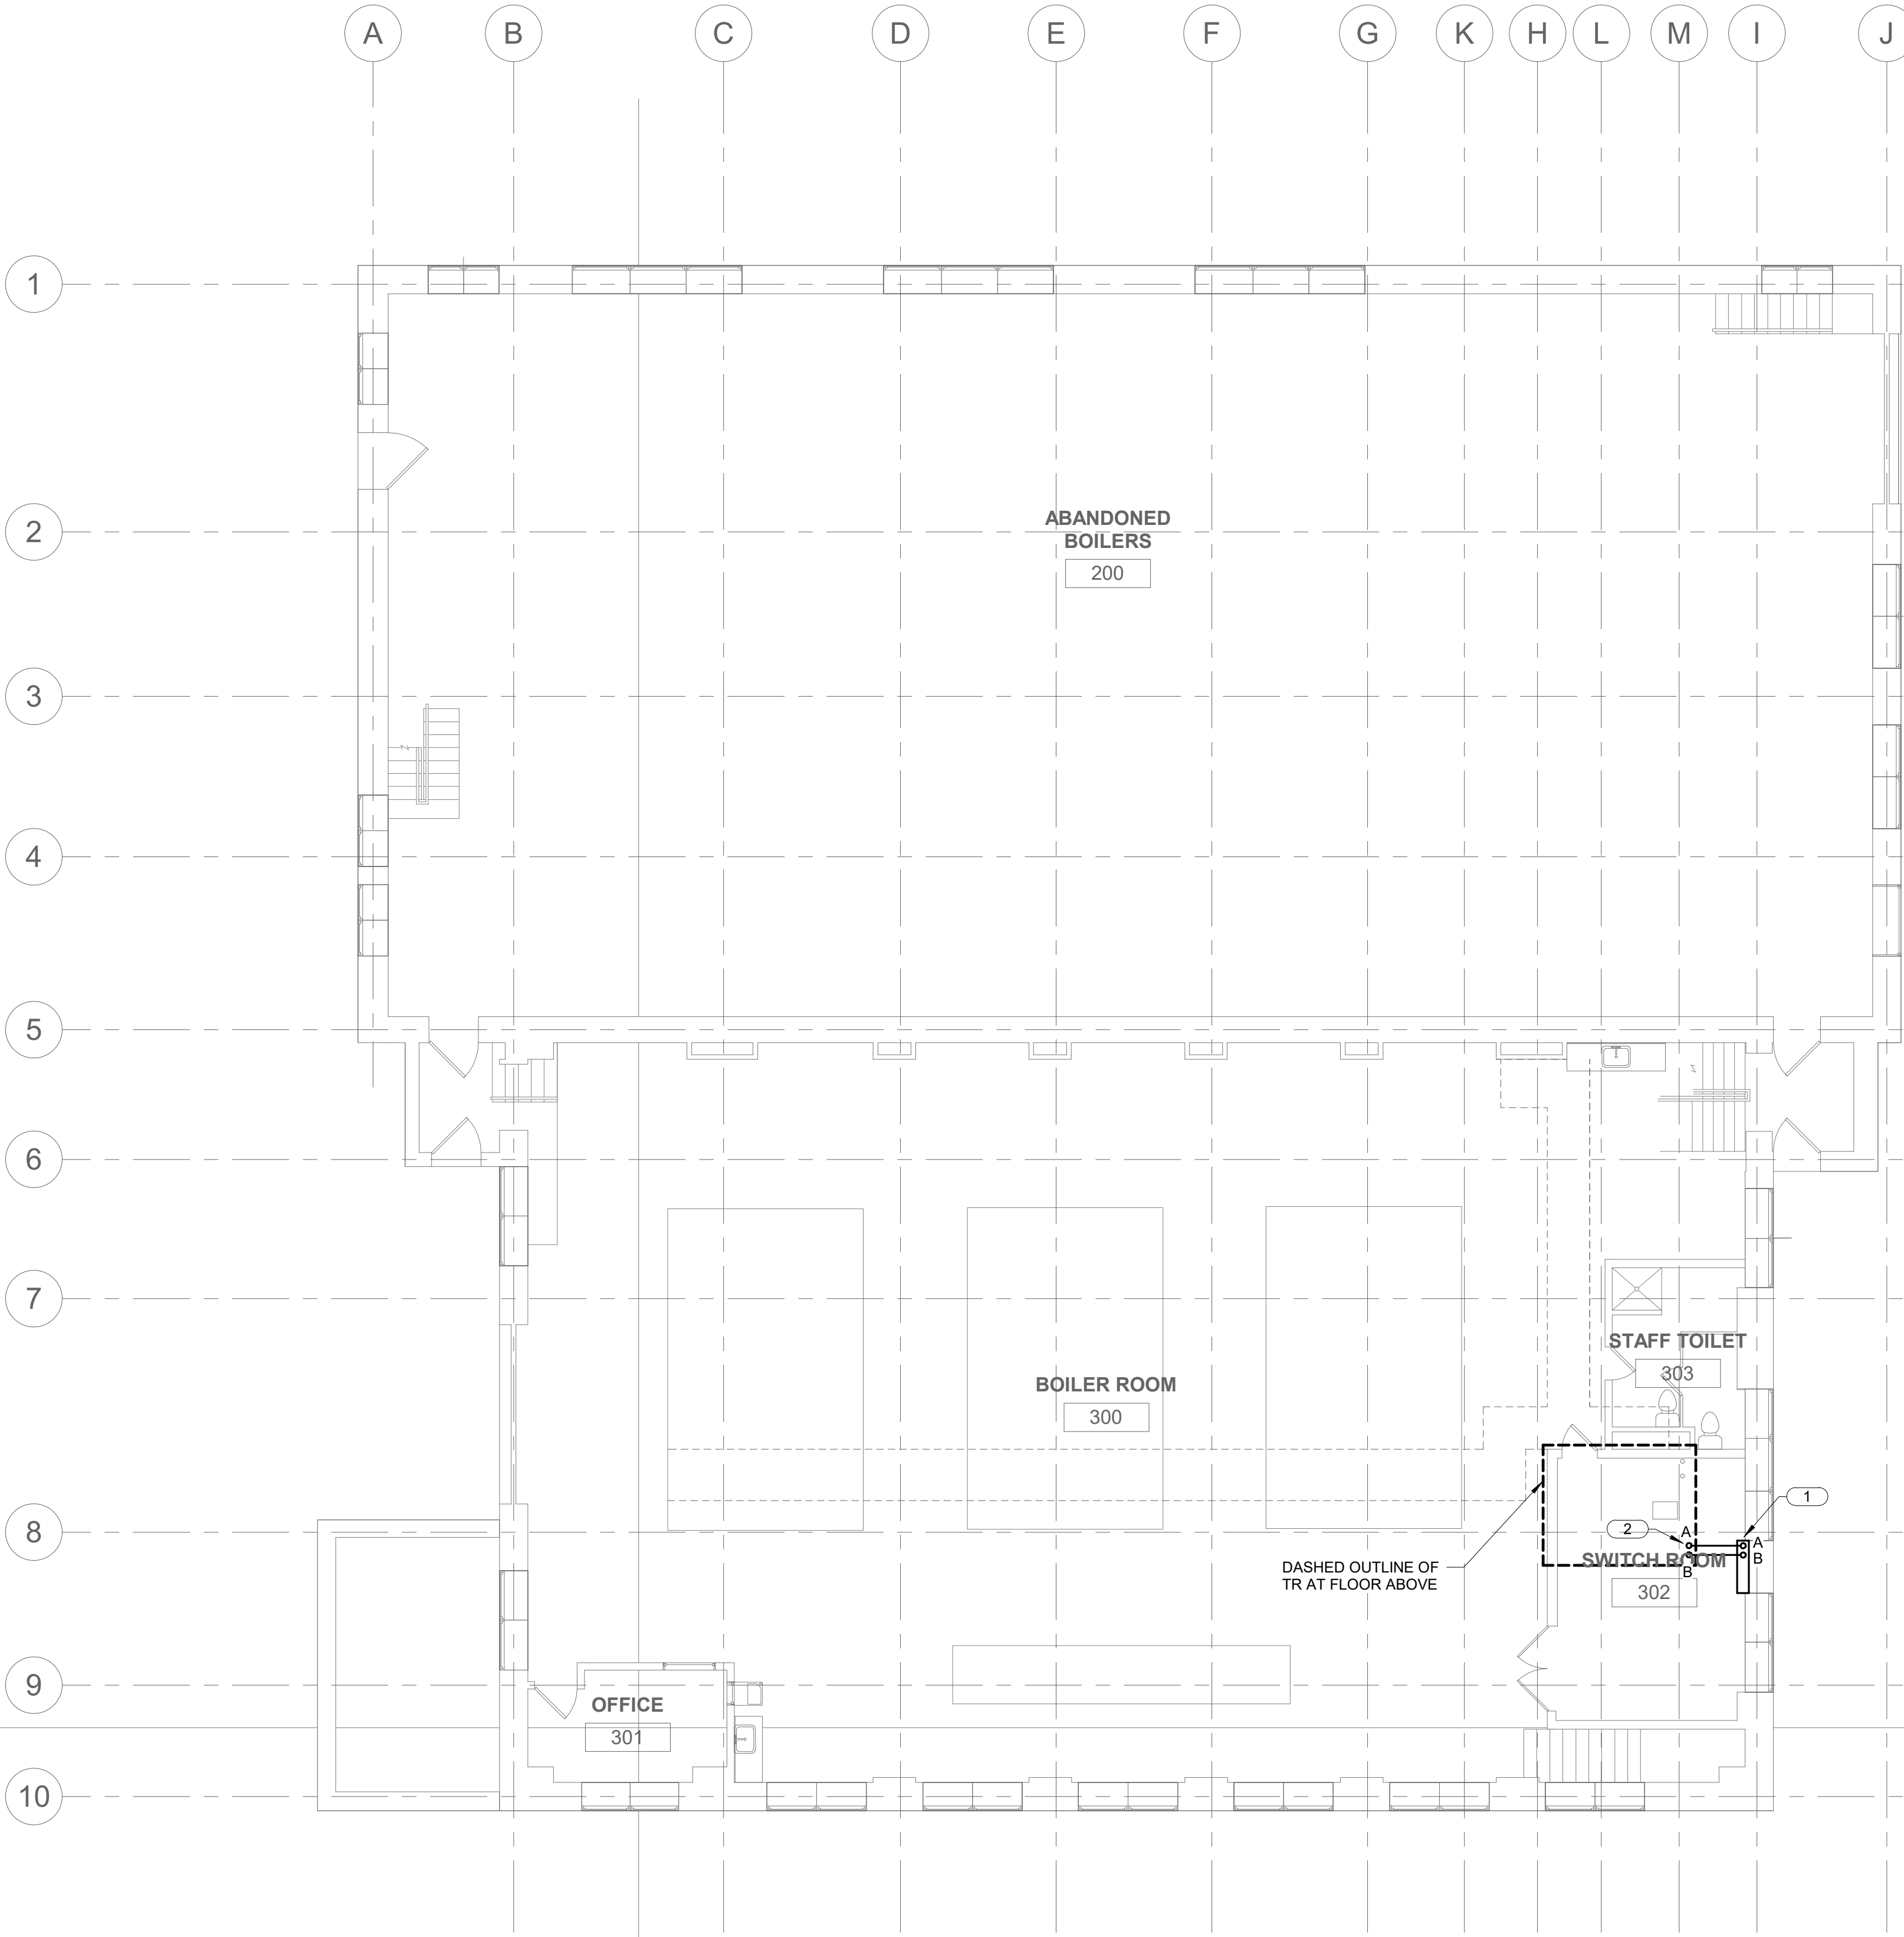


1

1/8" = 1'-0"


LEVEL 02 PLAN - TECHNOLOGY

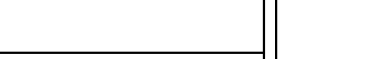		CONSULTANT	ARCHITECT/ENGINEER OF RECORD	STAMP	Office of Construction and Facilities Management	Drawing Title	Phase	Project Title	Project Number	
		ENGINEERING DISCIPLINE:	A/E:			BUILDING 15-LEVEL 02 PLAN - TECHNOLOGY	100% CONSTRUCTION DOCUMENTS	EHRM INFRASTRUCTURE UPGRADES - HAMPTON	509-22-700	
		 225 W WASHINGTON STREET SUITE 2700 CHICAGO, IL 60606 P: 312.294.0501 F: 312.294.0003 PROJECT #22010109.00	SPEES DESIGN BUILD 23830 PACIFIC HIGHWAY S. SUITE 203 KENT, WA 98032			 SPEESDESIGNBUILD	Approved:	FULLY SPRINKLERED	Location	Drawing Number
										HAMPTON VA MEDICAL CENTER, HAMPTON, VIRGINIA
Revisions:	Date:				VA		U.S. Department of Veterans Affairs	Issue Date	Checked	Drawn
							05/09/2025	EW	IMEG	

KEY NOTES: C #
1. ROUTE CONDUITS UP TO HEIGHT ABOVE CABLE TRAY. CONTINUE ROUTE OF NEW FIBER CABLES OVER TO TELECOM RACK.

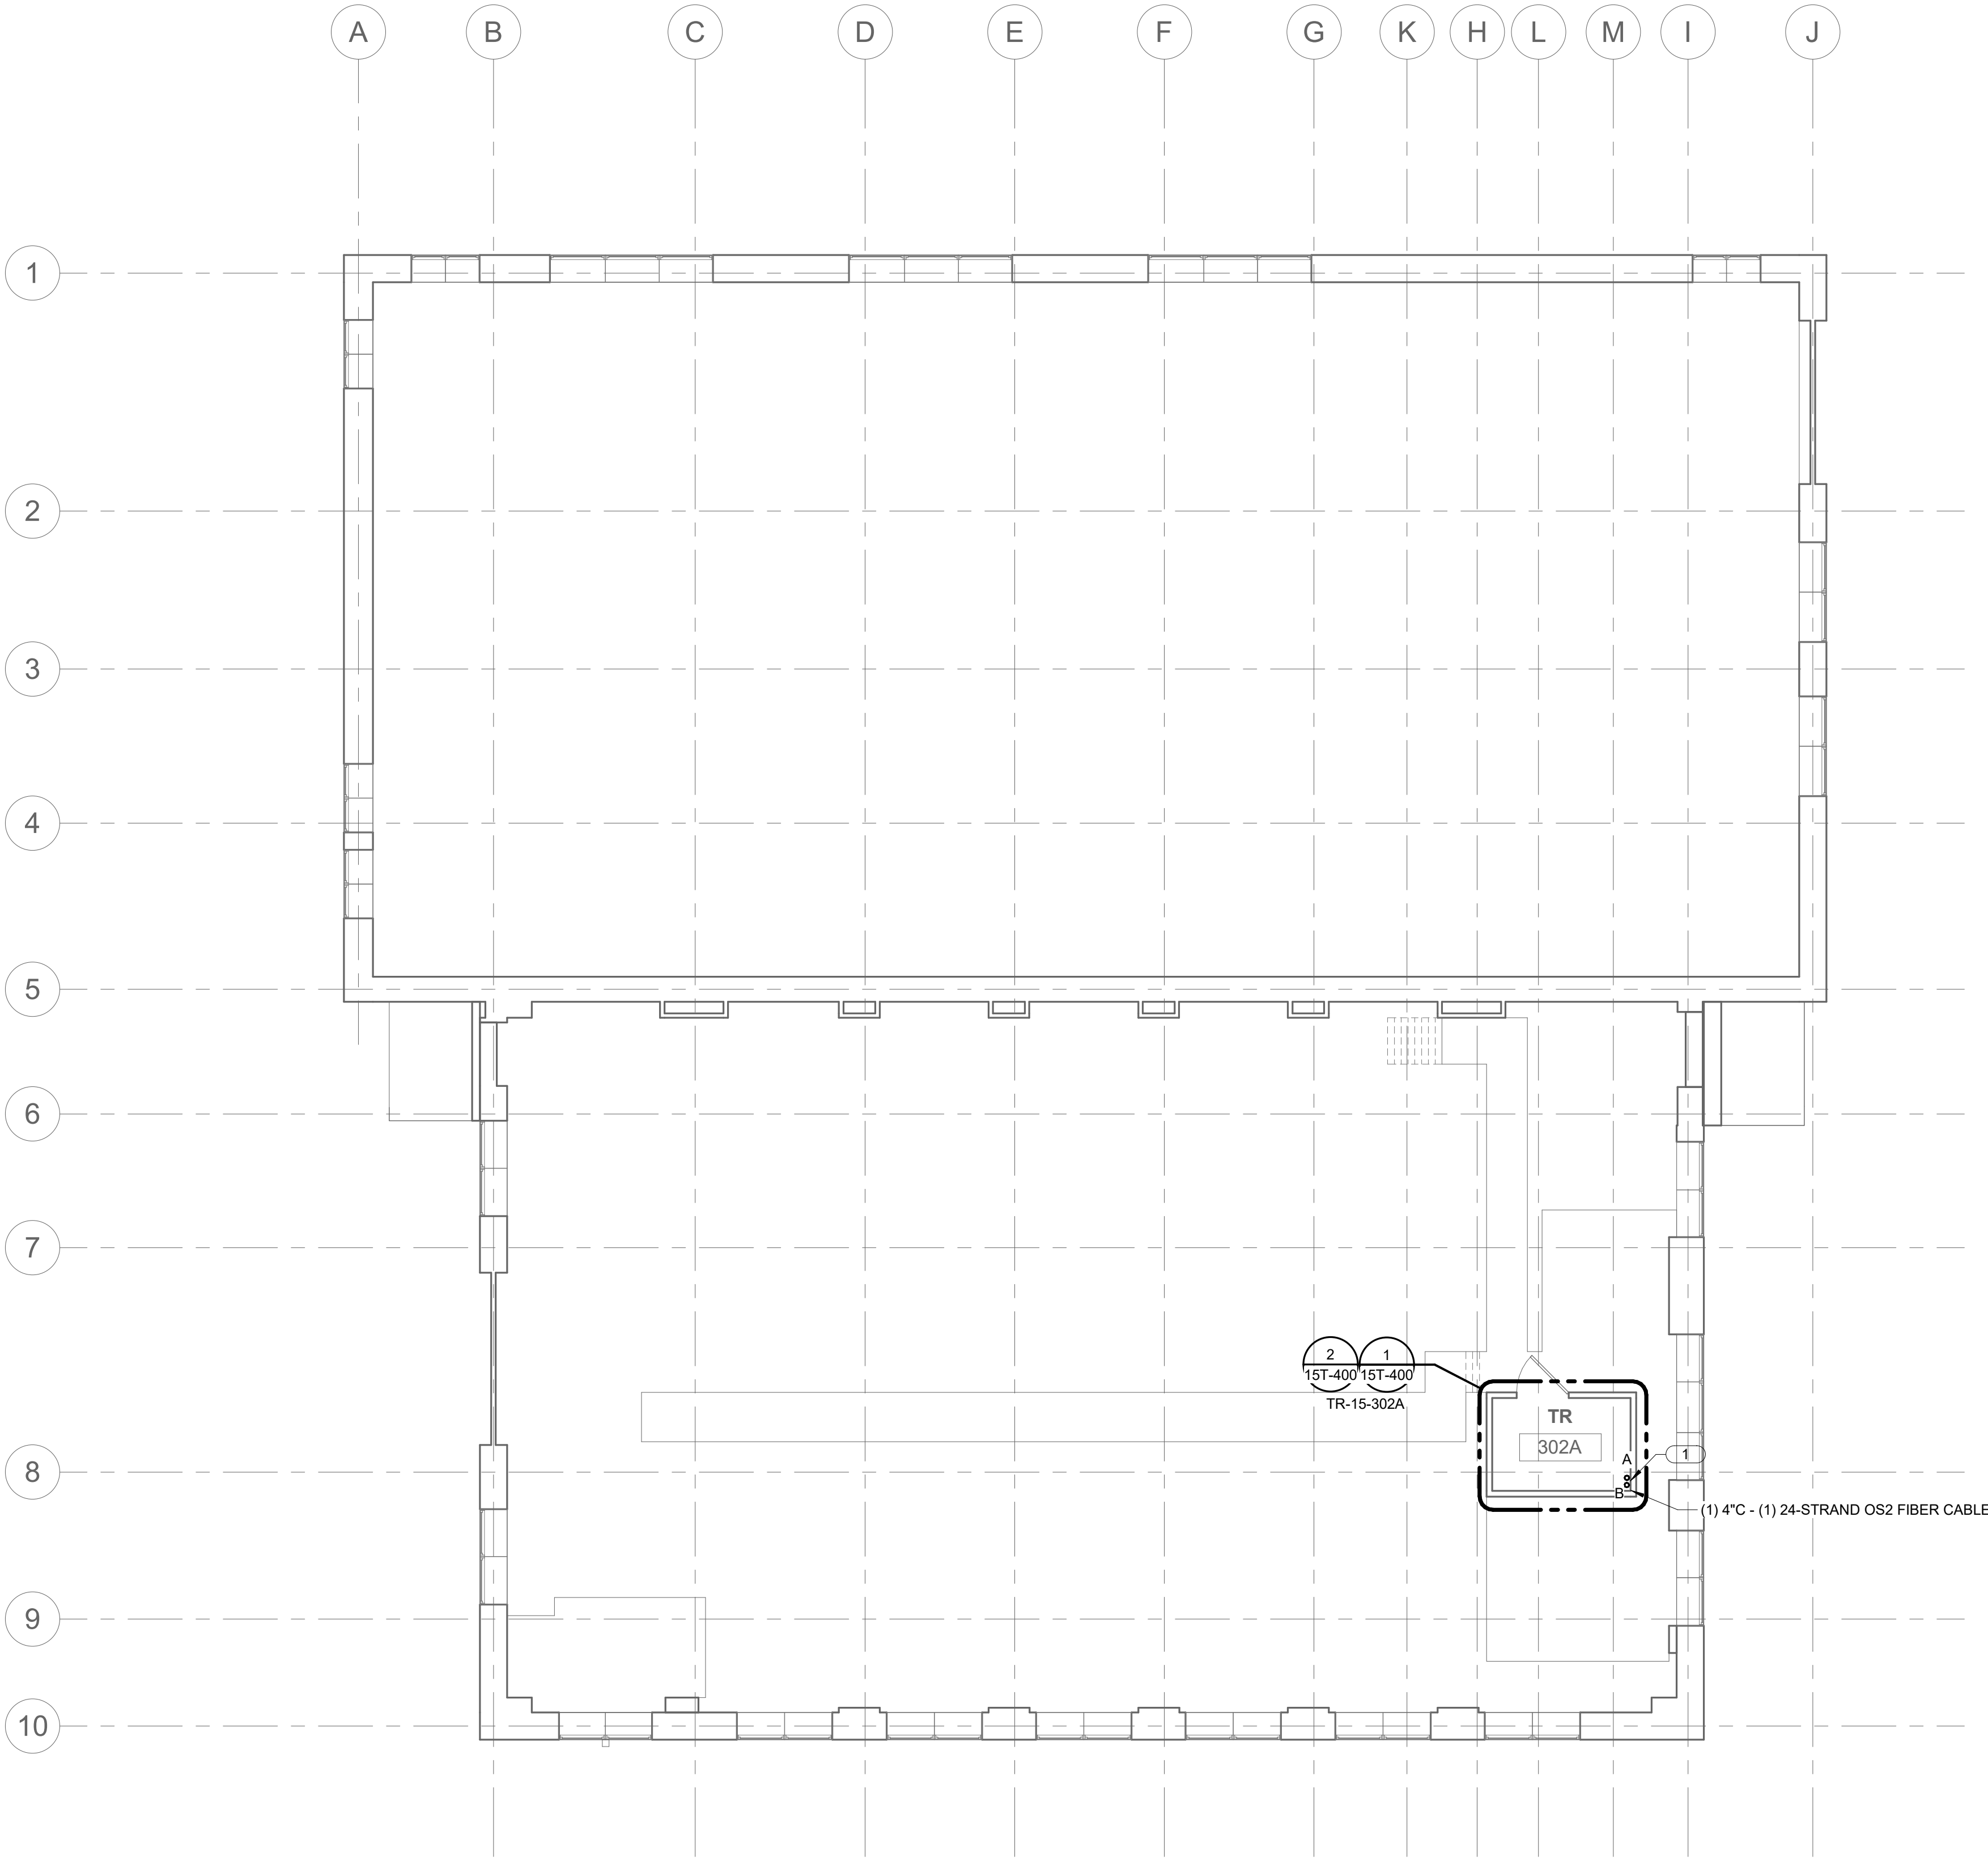

 1 CATWALK LEVEL PLAN - TECHNOLOGY
1/8" = 1'-0"

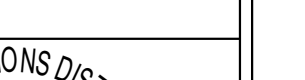		CONSULTANT	ARCHITECT/ENGINEER OF RECORD	STAMP	Office of Construction and Facilities Management	Drawing Title	Phase	Project Title	Project Number		
		ENGINEERING DISCIPLINE:	A/E:			BUILDING 15-CATWALK LEVEL PLAN - TECHNOLOGY	100% CONSTRUCTION DOCUMENTS	EHRM INFRASTRUCTURE UPGRADES - HAMPTON	509-22-700		
		 225 W WASHINGTON STREET SUITE 2700 CHICAGO, IL 60606 P: 312.294.0501 F: 312.294.0003 PROJECT #22010109.00	 SPEEDESIGNBUILD			 RCDD	Approved:	FULLY SPRINKLERED	Location	Building Number	
Revisions:	Date:				VA U.S. Department of Veterans Affairs			HAMPTON VA MEDICAL CENTER, HAMPTON, VIRGINIA	Drawing Number		
								Issue Date 05/09/2025	Checked EW	Drawn IMEG	15T-203
											636 of 713

BM 360/509-22-700
VA Hampton
E:\1509-22-700\B15T_101.rvt
8/13/2025 12:42:14 PM

Revisions:	Date:

CONSULTANT
ENGINEERING DISCIPLINE:

225 W WASHINGTON STREET SUITE 2700 CHICAGO, IL 60606 P: 312.294.0501 F: 312.294.0003 PROJECT #22010109.00

ARCHITECT/ENGINEER OF RECORD
A/E:
SPEES DESIGN BUILD 23830 PACIFIC HIGHWAY S. SUITE 203 KENT, WA 98032
 SPEESDESIGNBUILD

STAMP


Office of Construction and Facilities Management
 U.S. Department of Veterans Affairs


Drawing Title
TECHNOLOGY ENLARGED PLANS
Approved:

Phase
100% CONSTRUCTION DOCUMENTS
FULLY SPRINKLERED

Project Title
EHRM INFRASTRUCTURE UPGRADES - HAMPTON
Location
HAMPTON VA MEDICAL CENTER, HAMPTON, VIRGINIA
Issue Date
05/09/2025
Checked
EW
Drawn
IMEG


Project Number
509-22-700
Building Number
Drawing Number
15T-400
637 of 713


- SHEET NOTES:**
1. REFER TO SITEPLAN TS001 FOR ADDITIONAL INFORMATION.
 2. REFER TO TS00 AND TS01 FOR CAMPUS OPTICAL FIBER CABLE RISER DIAGRAMS.
 3. REFER TO 27T400 FOR HANDHOLE DETAIL.
 4. NEW BACKBONE OPTICAL FIBER CABLES SHALL BE INDOOR/OUTDOOR TYPE.
 5. ALL BACKBONE OPTICAL FIBER CABLE PATHWAYS SHALL BE NEW. DO NOT RE-USE EXISTING BACKBONE CABLE PATHWAYS FOR NEW BACKBONE CABLES.
 6. TRANSITION PVC CONDUITS TO GRC IN CRAWL SPACE OR EXPOSED EXTERIOR LOCATIONS. TRANSITION TO EMT CONDUITS AT INTERIOR OF BUILDING. SEAL ALL PENETRATIONS TO MAINTAIN FIRE-RATINGS OF WALL, CEILING AND FLOORS.
- KEY NOTES: (C #)**
1. PROVIDE PULLBOX ON EXTERIOR WALL AT HEIGHT ABOVE FINISHED CEILING. ROUTE CONDUIT UP WALL INTO PULLBOX. PROVIDE PENETRATION THRU EXTERIOR WALL AND ROUTE CONDUITS AT CEILING HEIGHT TO LOCATION OF NEW TE IN ROOM #108.

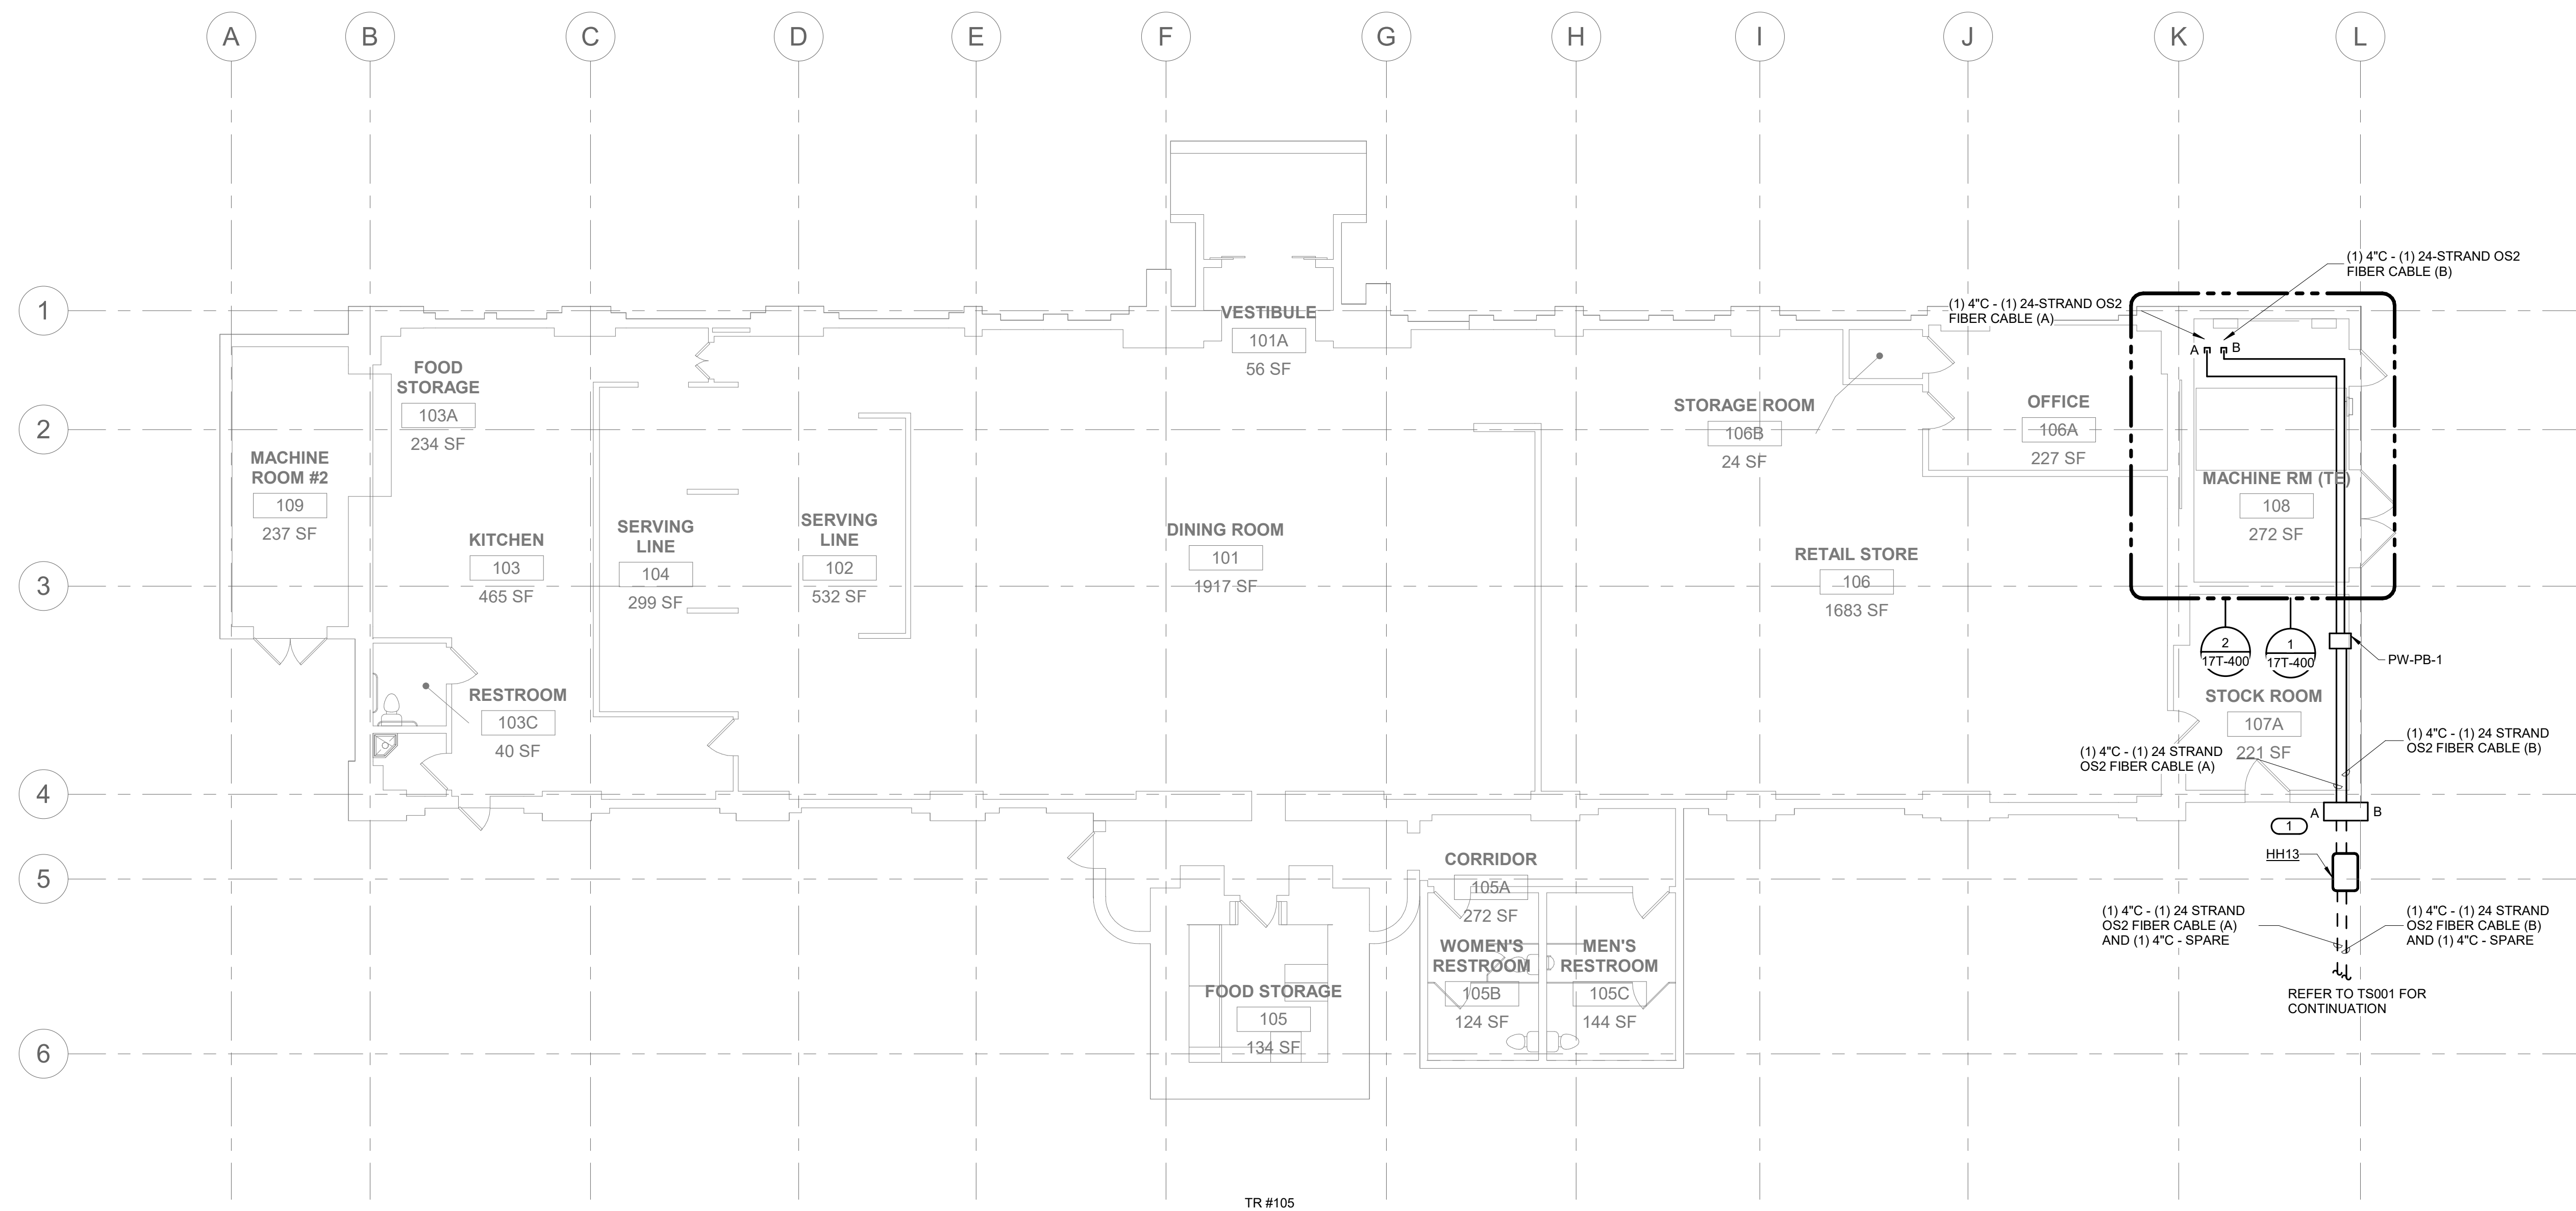

1 LEVEL 01 PLAN - TECHNOLOGY
1/8" = 1'-0"

BM 360/509-22-700
VAHampton
E:\17T-201\17T-201.dwg
8/13/2025 12:53:37 PM

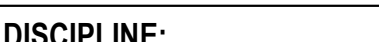		CONSULTANT	ARCHITECT/ENGINEER OF RECORD	STAMP	Office of Construction and Facilities Management	Drawing Title	Phase	Project Title			Project Number
		ENGINEERING DISCIPLINE:	A/E:			BLDG.17 LEVEL 01 PLAN - TECHNOLOGY	100% CONSTRUCTION DOCUMENTS	EHRM INFRASTRUCTURE UPGRADES - HAMPTON	509-22-700		
		 www.imegcorp.com 225 W WASHINGTON STREET SUITE 2700 CHICAGO, IL 60606 P: 312.294.0501 F: 312.294.0003 PROJECT #22010109.00	SPEES DESIGN BUILD 23830 PACIFIC HIGHWAY S. SUITE 203 KENT, WA 98032				Building Number				
							17				
Revisions:	Date:		 SPEESDESIGNBUILD	RCDD	VA U.S. Department of Veterans Affairs	Approved:	FULLY SPRINKLERED	Location	HAMPTON VA MEDICAL CENTER, HAMPTON, VIRGINIA		Drawing Number
								Issue Date	Checked	Drawn	17T-201
								05/09/2025	EW	IMEG	638 of 713

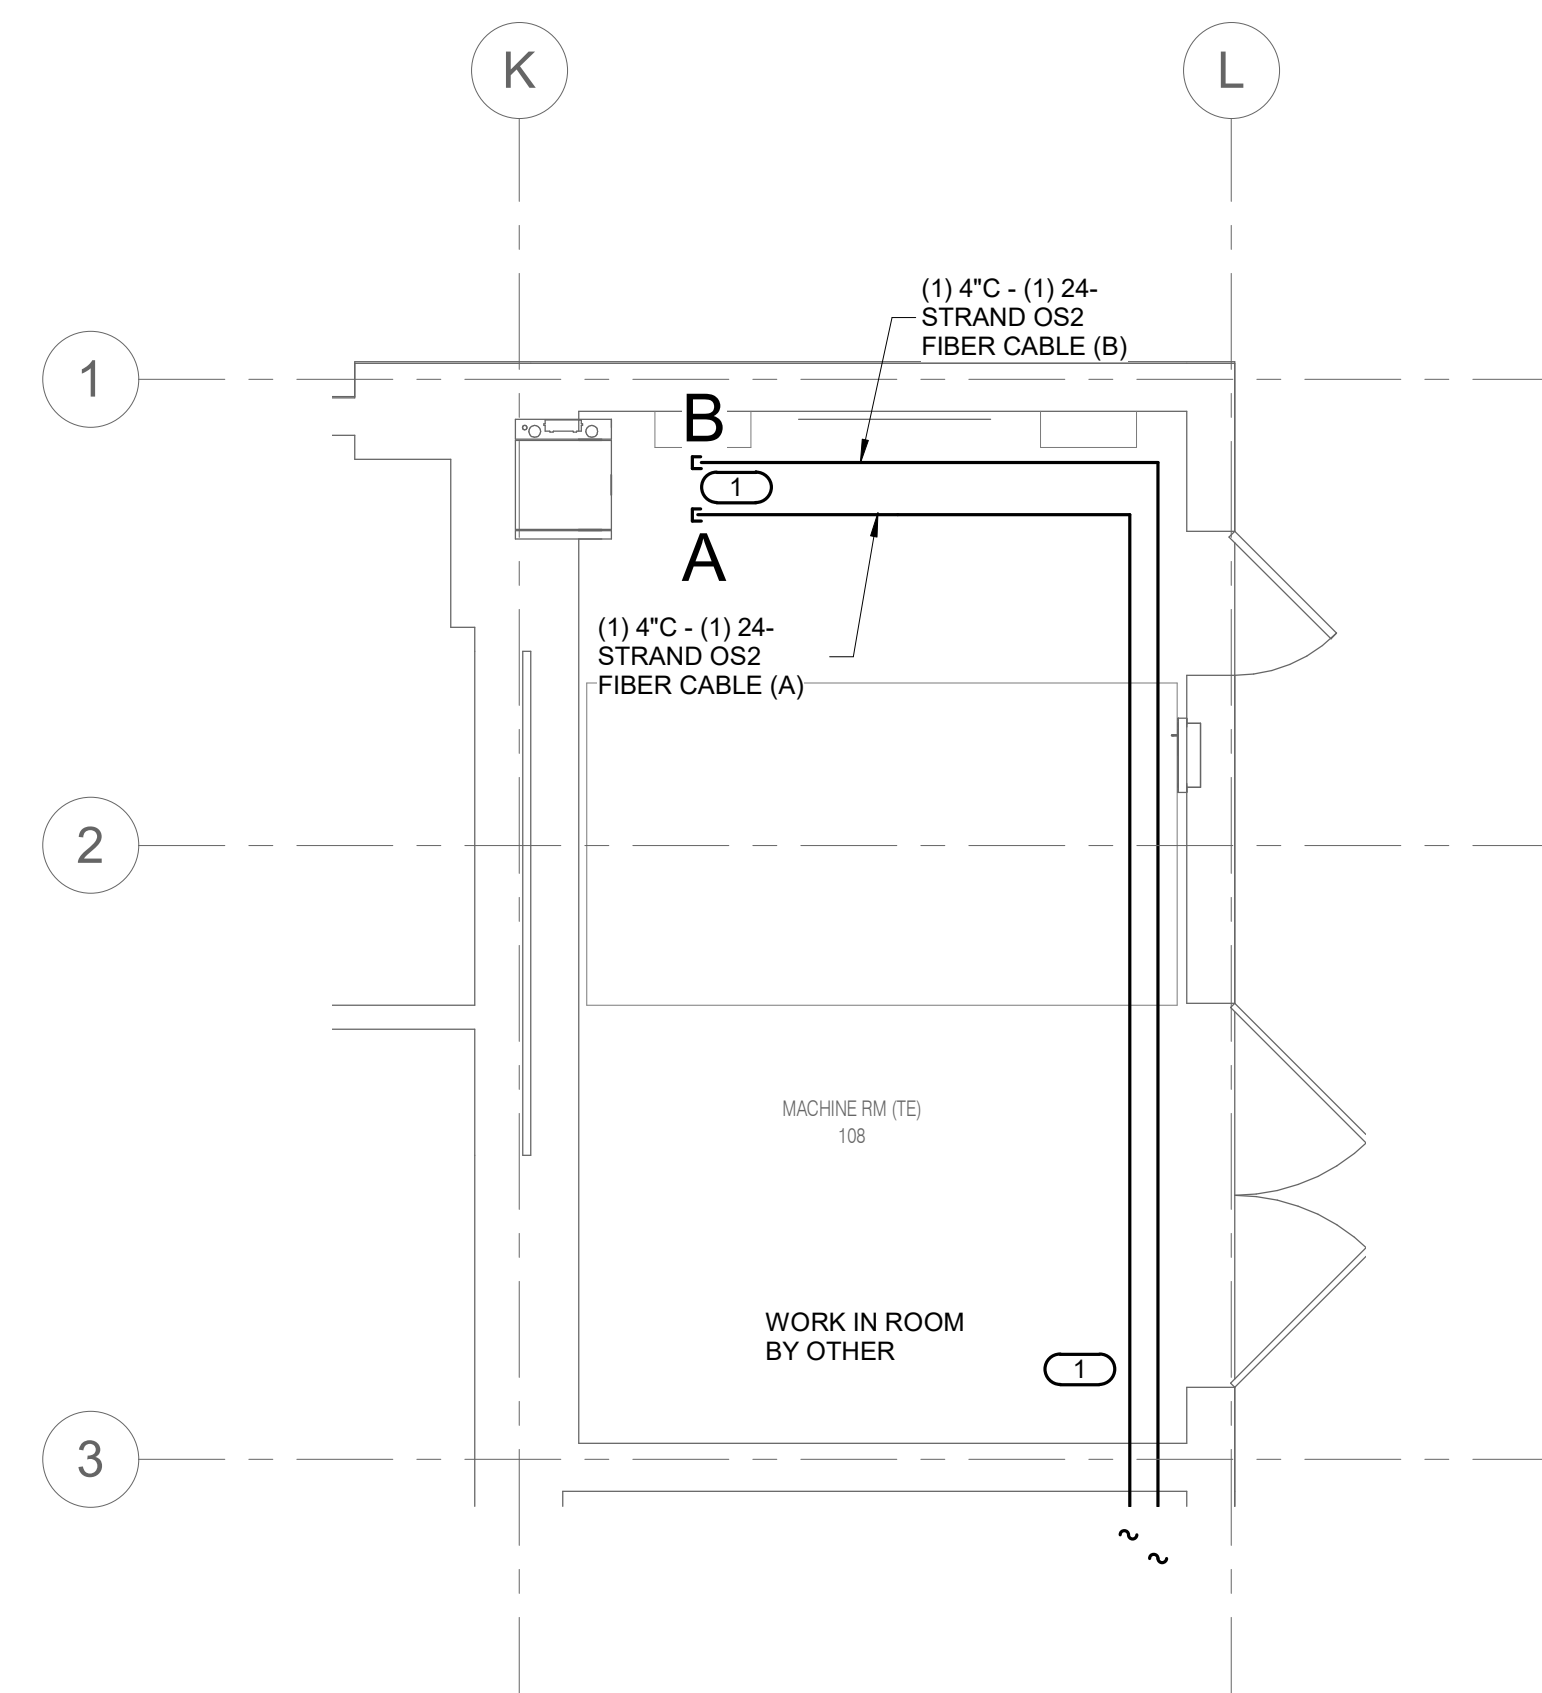

 TELECOM ENCLOSURE ENLARGEMENT TE #108


1/4" = 1'-0"

NOTES:

1. REFER TO ELECTRICAL DRAWINGS FOR ROOM LAYOUT AND RACK ELEVATIONS.
2. ROUTE OPTICAL FIBER CABLE TO OVERHEAD CABLE TRAY AND TERMINATE IN FIBER DISTRIBUTION CABINET.

KEY NOTES: #


1. THROUGH WALL PENETRATION FOR BACKBONE CONDUIT. OPTICAL FIBER CABLE CONTINUES IN CONDUIT TO ABOVE TELECOM ENCLOSURE.

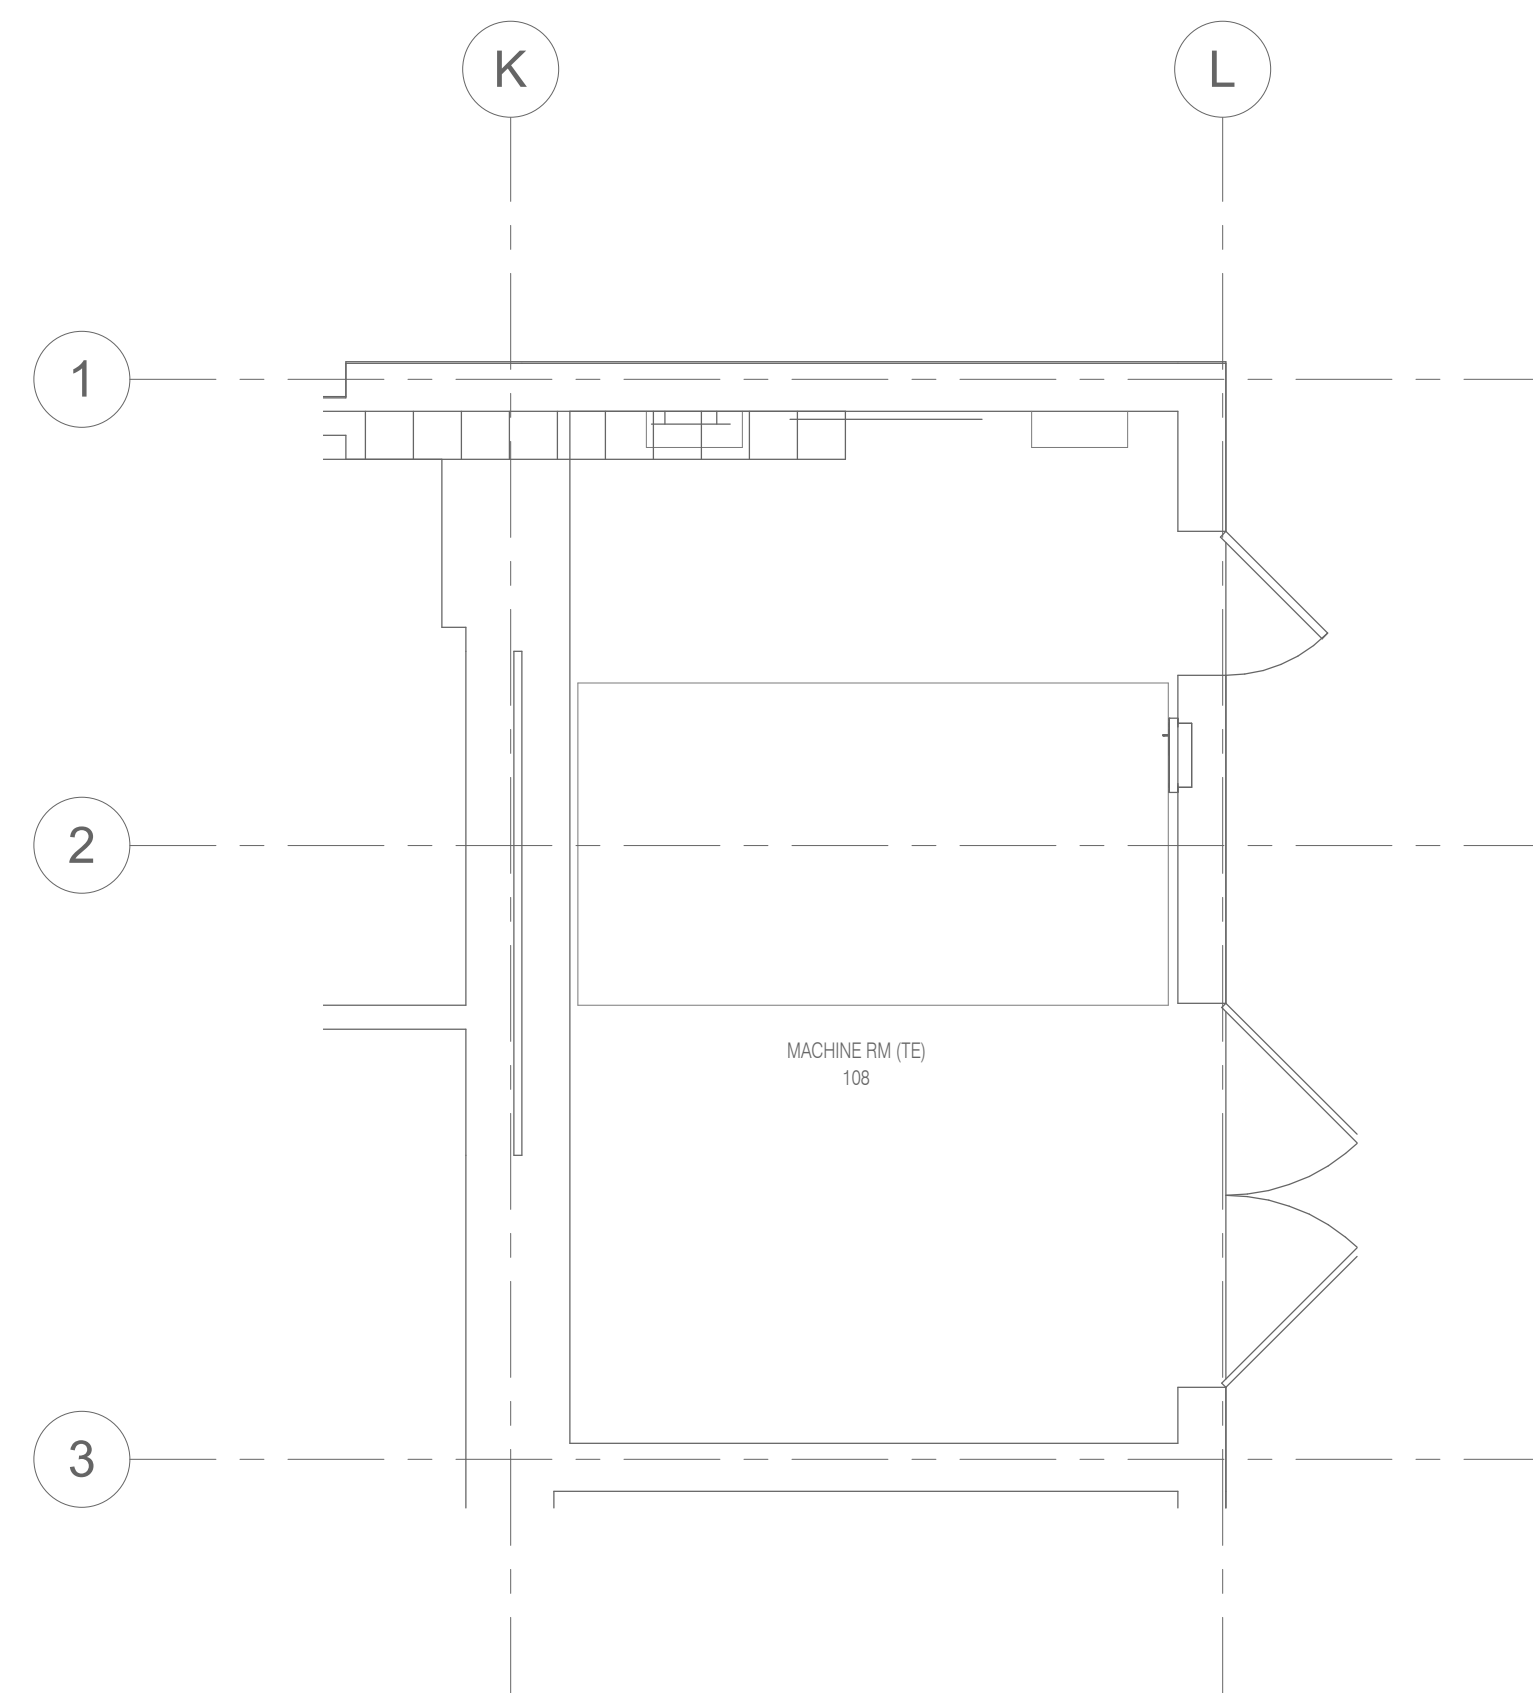

 2 TELECOM ENCLOSURE PATHWAY TE #108
1/4" = 1'-0"

NOTES:

1. REFER TO ELECTRICAL DRAWINGS FOR ROOM LAYOUT AND RACK ELEVATIONS
2. ROUTE OPTICAL FIBER CABLES TO OVERHEAD CABLE TRAY AND TERMINATE IN FIBER DISTRIBUTION CABINET

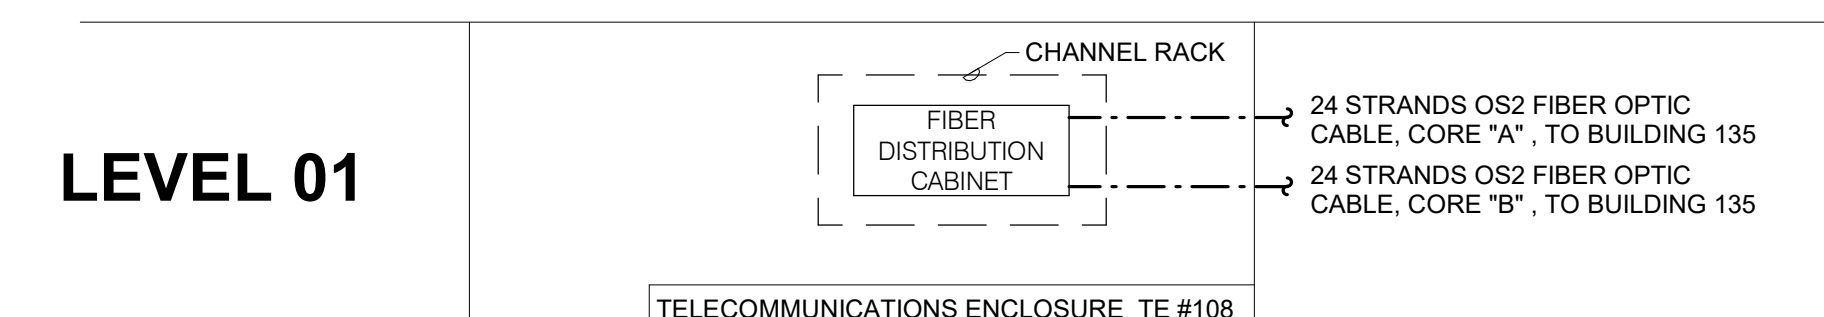

3 FIBER RISER DIAGRAM

NO SCALE

NOTES:

1. THIS RISER IS DIAGRAMMATIC AND MAY NOT SHOW ACTUAL ROUTING OR QUANTITIES OF MATERIALS SHOWN. THIS RISER IS SHOWN FOR CLARIFICATION OF CONNECTION(S), LOCATIONS AND CABLE TYPE. ALL INFORMATION OUTLETS ARE TYPICAL OF THE OUTLETS IN THE AREA SHOWN. REFER TO FLOOR PLANS FOR MORE SPECIFIC ROUTING INFORMATION. REFER TO SPECIFICATIONS FOR ADDITIONAL REQUIREMENTS.
2. REFER TO ELECTRICAL DRAWINGS FOR CHANNEL RACK AND FIBER OPTIC DISTRIBUTION CABINET SPECIFICATIONS

--	--	

- SHEET NOTES:
1. REFER TO SITEPLAN TS001 FOR ADDITIONAL INFORMATION.


2. REFER TO TS00 AND TS01 FOR CAMPUS OPTICAL FIBER CABLE RISER DIAGRAMS.

3. REFER TO 2/T400 FOR HANDHOLE DETAIL.

4. NEW BACKBONE OPTICAL FIBER CABLES SHALL BE INDOOR/OUTDOOR TYPE.

5. ALL BACKBONE OPTICAL FIBER CABLE PATHWAYS SHALL BE NEW. DO NOT RE-USE EXISTING BACKBONE CABLE PATHWAYS FOR NEW BACKBONE CABLES.

6. TRANSITION PVC CONDUITS TO GRC IN CRAWL SPACE OR EXPOSED EXTERIOR LOCATIONS. TRANSITION TO EMT CONDUITS AT INTERIOR OF BUILDING. SEAL ALL PENETRATIONS TO MAINTAIN FIRE-RATINGS OF WALL, CEILING AND FLOORS.
- KEY NOTES: C #
1. PROVIDE PULLBOX ON EXTERIOR WALL AT HEIGHT ABOVE FINISHED CEILING. ROUTE CONDUIT UP WALL INTO PULLBOX. PROVIDE PENETRATION THRU WALL AND ROUTE CONDUIT THRU WALL ABOVE FINISHED CEILING AND OVER TO TE #103 IN STORAGE ROOM.

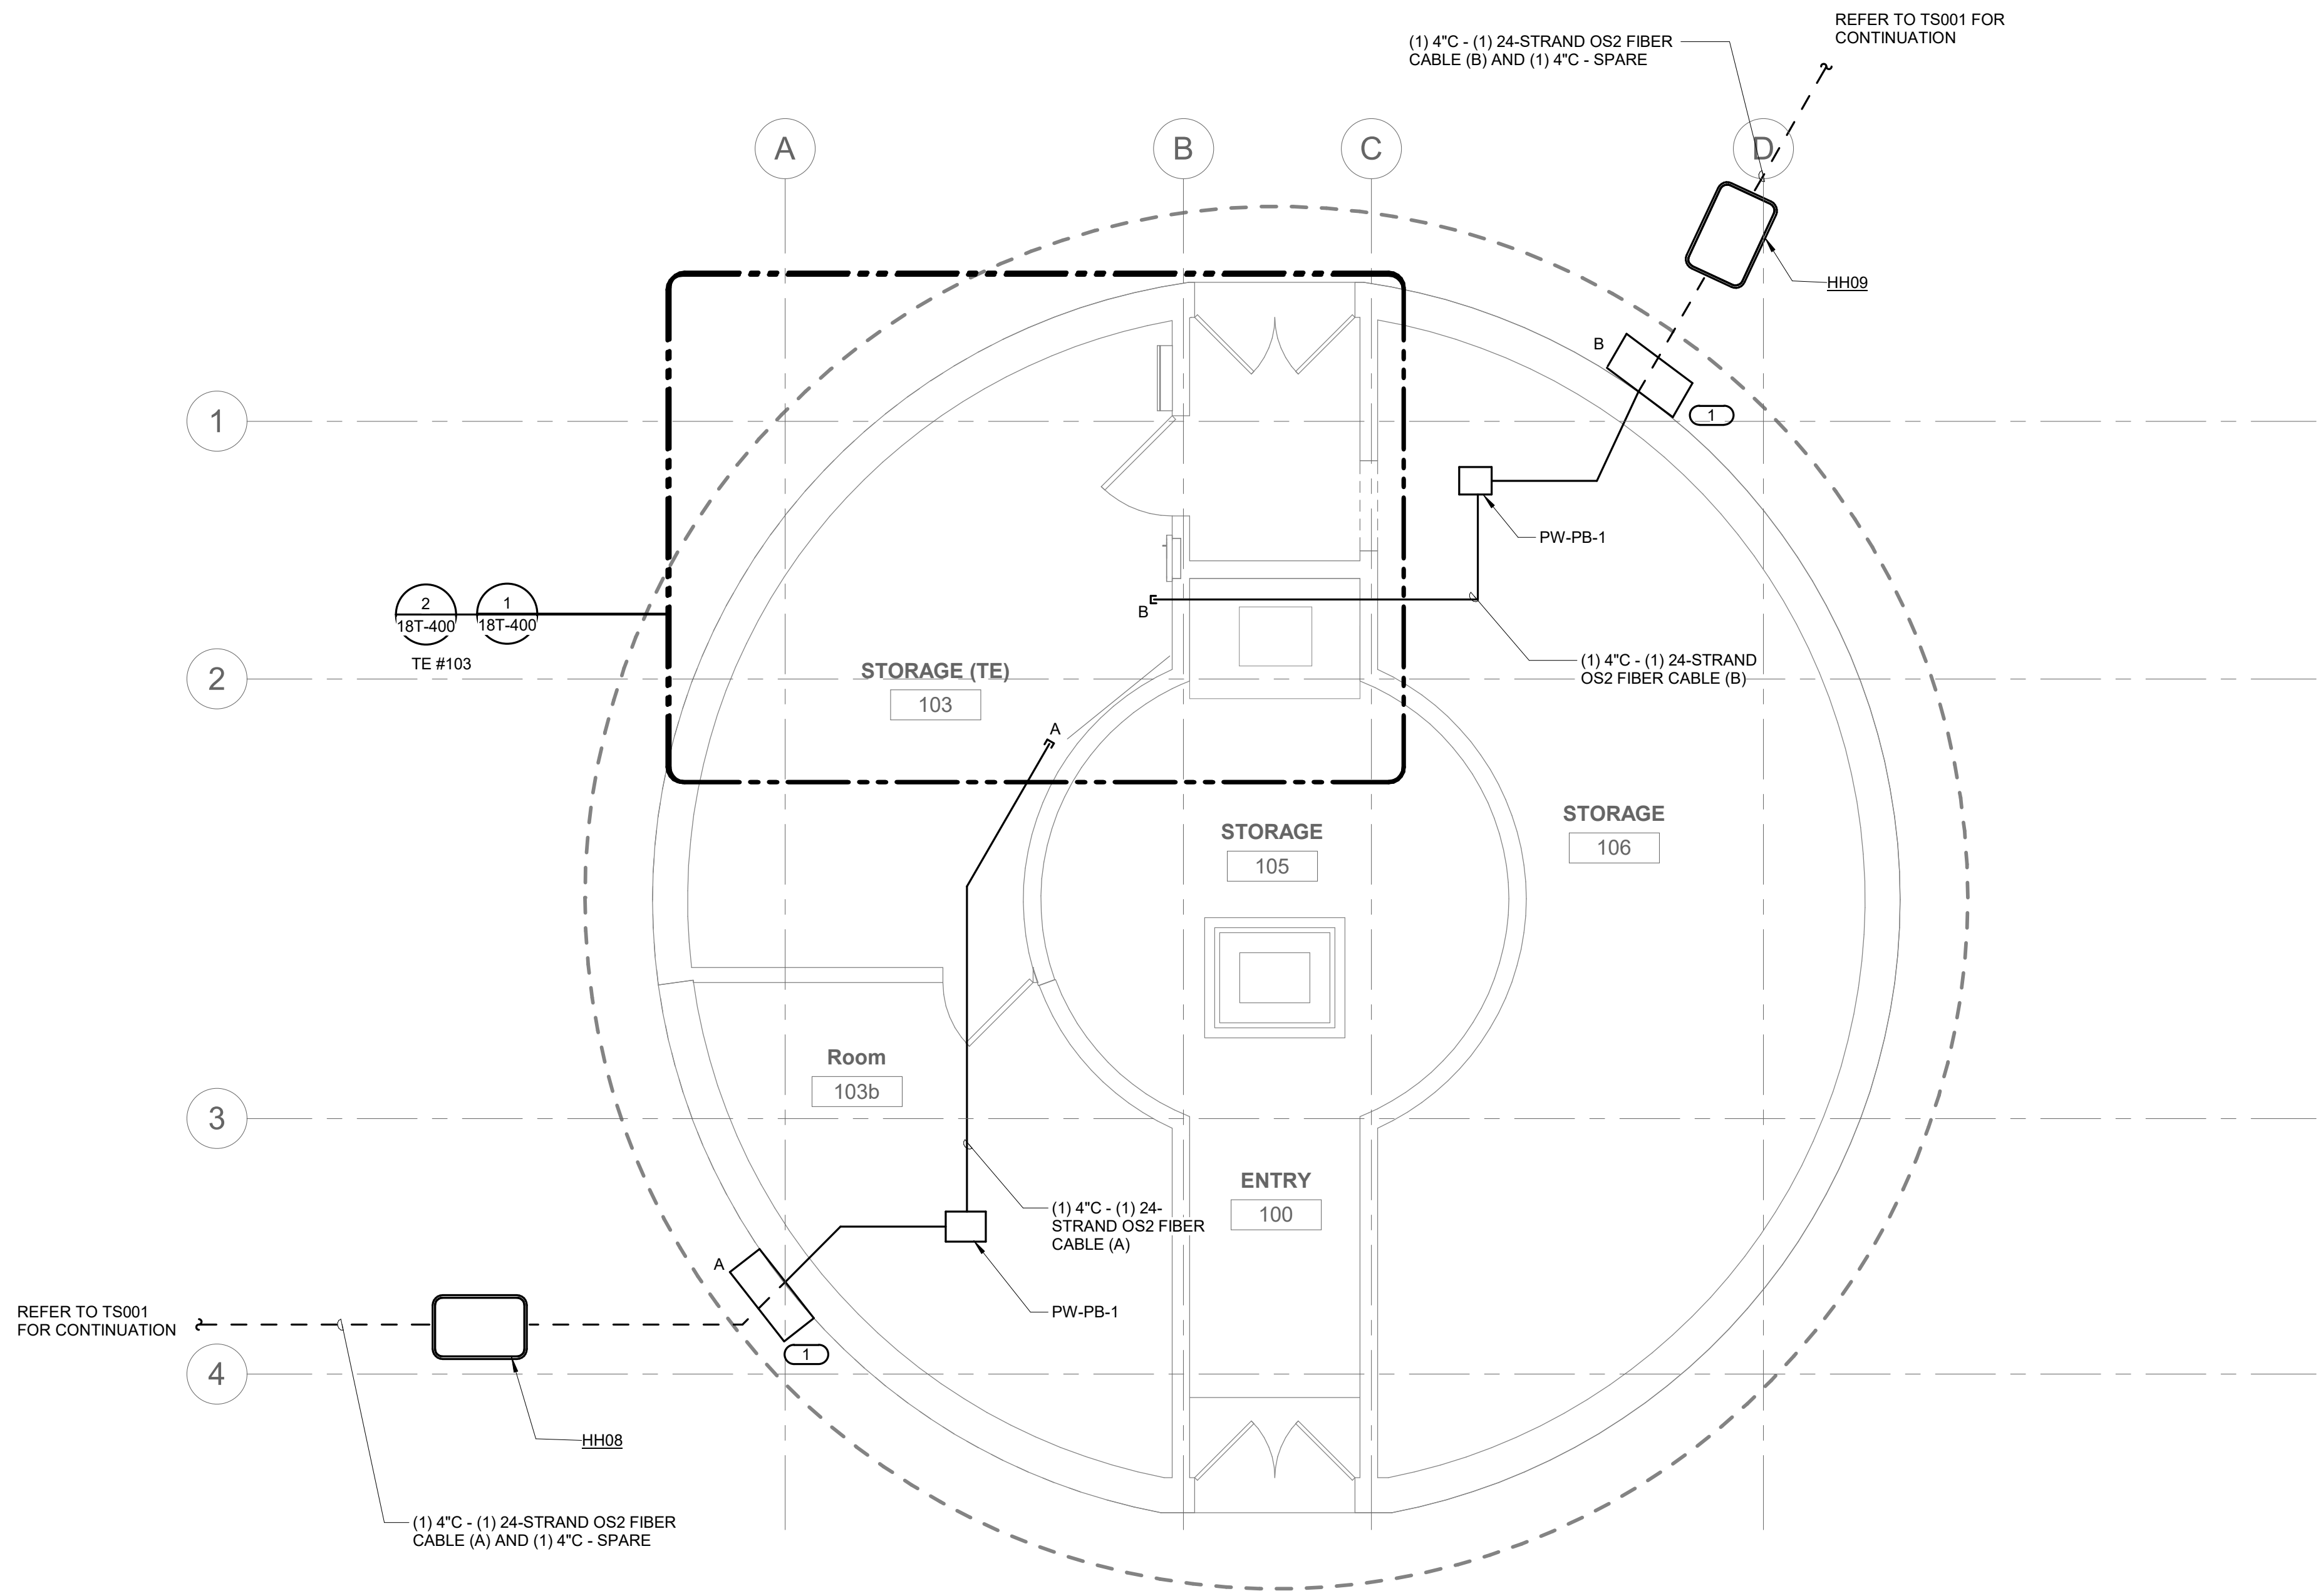

 **1** **LEVEL 01 PLAN - TECHNOLOGY**
1/4" = 1'-0"

--	--	

BM 360/509-22-700
VAHAMPTON
E:\18T-400\18T-400\18T-400.dwg

8/13/2025 1:02:32 PM

VA FORM 08 - 6231

Revisions:	Date:

CONSULTANT
ENGINEERING DISCIPLINE:
IMEG
225 W WASHINGTON STREET SUITE 2700 CHICAGO, IL 60609 P: 312.294.0501 F: 312.294.0003 PROJECT #22010109.00

ARCHITECT/ENGINEER OF RECORD
A/E:
SPEES DESIGN BUILD 23830 PACIFIC HIGHWAY S. SUITE 203 KENT, WA 98032
SDB SPEESDESIGNBUILD

STAMP
Bicsi ES&C W&B-J Reg. No. 1519026 EXPIRES 01-01-2025 RCDD

Office of Construction and Facilities Management
VA U.S. Department of Veterans Affairs

Drawing Title
BLDG.18 TECHNOLOGY DETAILS AND DIAGRAMS
Approved:

Phase
100% CONSTRUCTION DOCUMENTS
FULLY SPRINKLERED

Project Title
EHRM INFRASTRUCTURE UPGRADES - HAMPTON
Location
HAMPTON VA MEDICAL CENTER, HAMPTON, VIRGINIA
Issue Date
05/09/2025
Checked
EW
Drawn
IMEG

Project Number
509-22-700
Building Number
18
Drawing Number
18T-400
641 of 713

NORTH

1

1/2" = 1'-0"


TELECOM ENCLOSURE ENLARGEMENT TE #103

NOTES:

1. REFER TO ELECTRICAL DRAWINGS FOR ROOM LAYOUT AND RACK ELEVATIONS.
2. ROUTE OPTICAL FIBER CABLE TO OVERHEAD CABLE TRAY AND TERMINATE IN FIBER DISTRIBUTION CABINET.

KEY NOTES: (#)

1. THROUGH WALL PENETRATION FOR BACKBONE CONDUIT. OPTICAL FIBER CABLE CONTINUES IN CONDUIT TO ABOVE TELECOM ENCLOSURE.

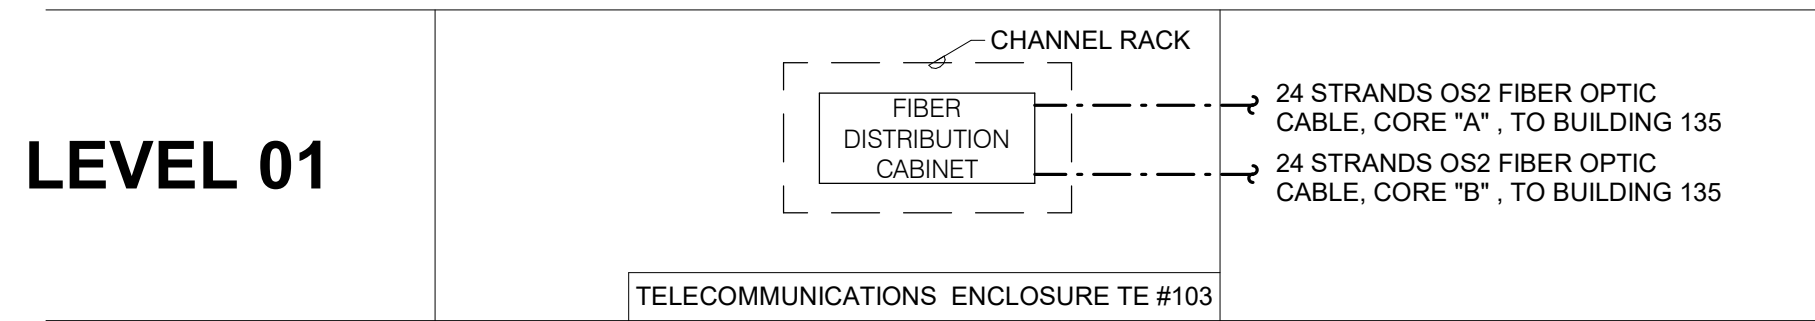

3

FIBER RISER DIAGRAM

NO SCALE

NOTES:



1. THIS RISER IS DIAGRAMMATIC AND MAY NOT SHOW ACTUAL ROUTING OR QUANTITIES OF MATERIALS SHOWN. THIS RISER IS SHOWN FOR CLARIFICATION OF CONNECTIONS, LOCATIONS AND CABLE TYPE. ALL INFORMATION OUTLETS ARE TYPICAL OF THE OUTLETS IN THE AREA SHOWN. REFER TO FLOOR PLANS FOR MORE SPECIFIC ROUTING INFORMATION. REFER TO SPECIFICATIONS FOR ADDITIONAL REQUIREMENTS.
2. REFER TO ELECTRICAL DRAWINGS FOR CHANNEL RACK AND FIBER OPTIC DISTRIBUTION CABINET SPECIFICATIONS

NORTH


2

1/2" = 1'-0"


TELECOM ENCLOSURE PATHWAY TE #103

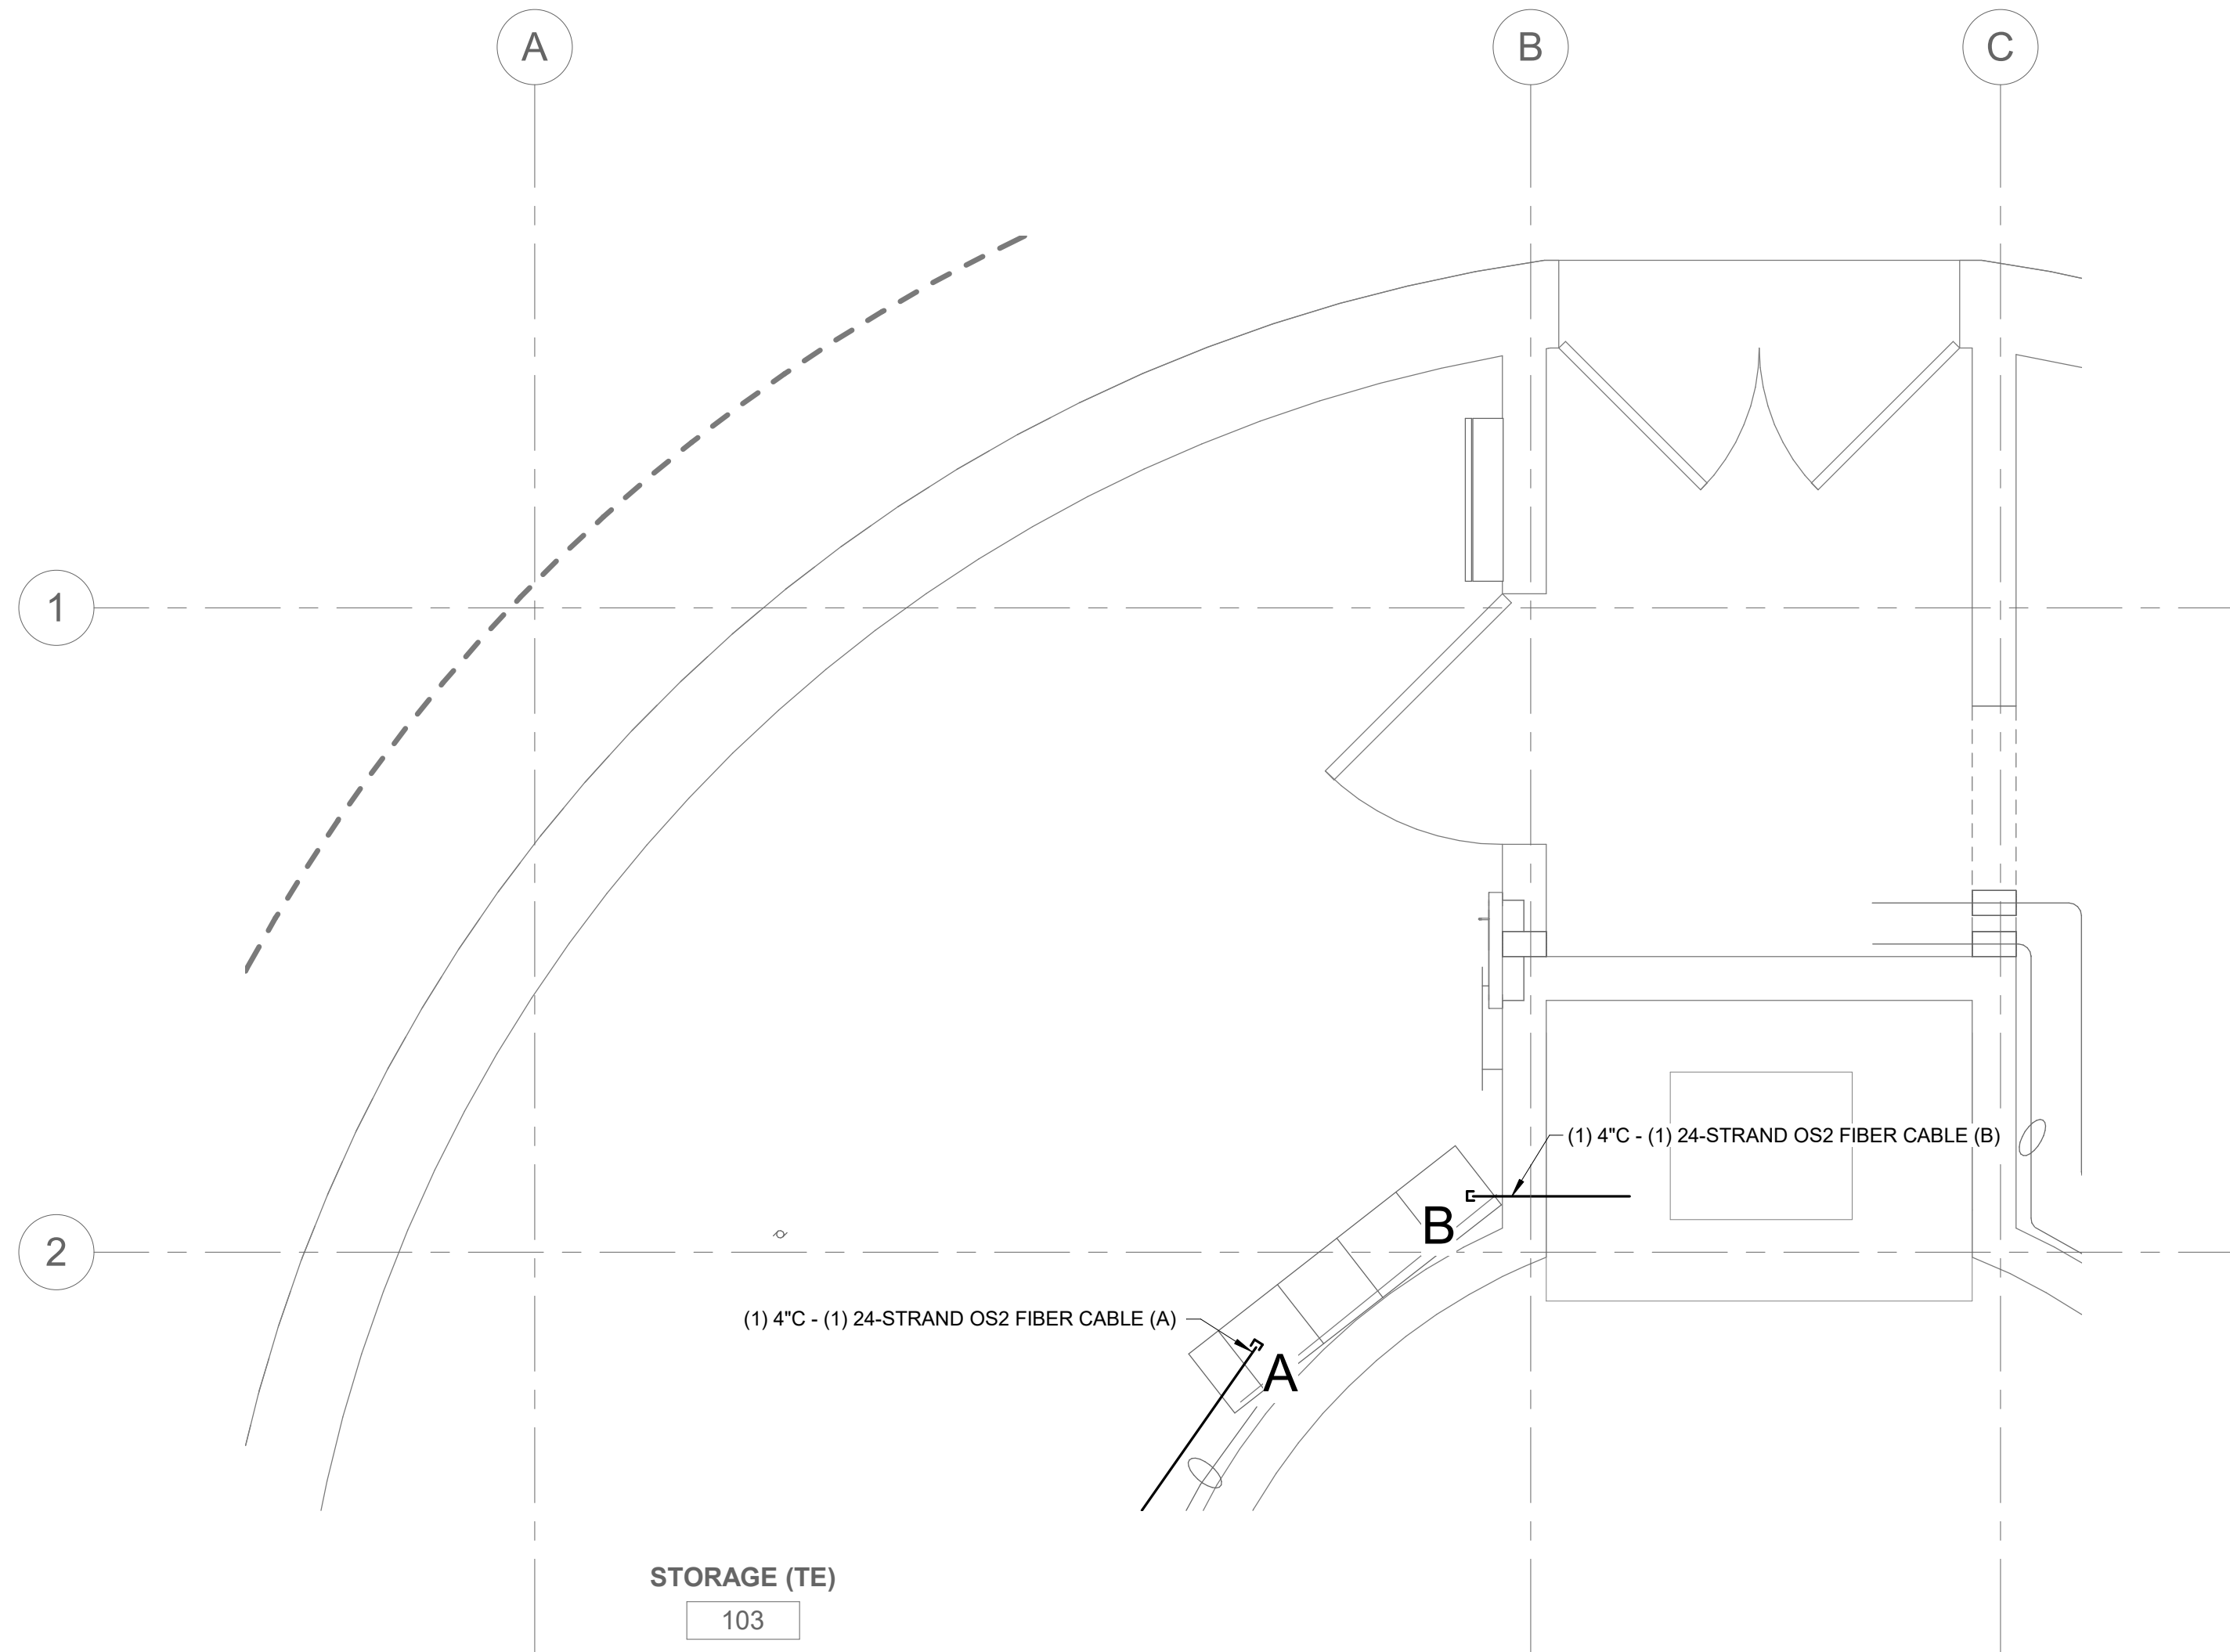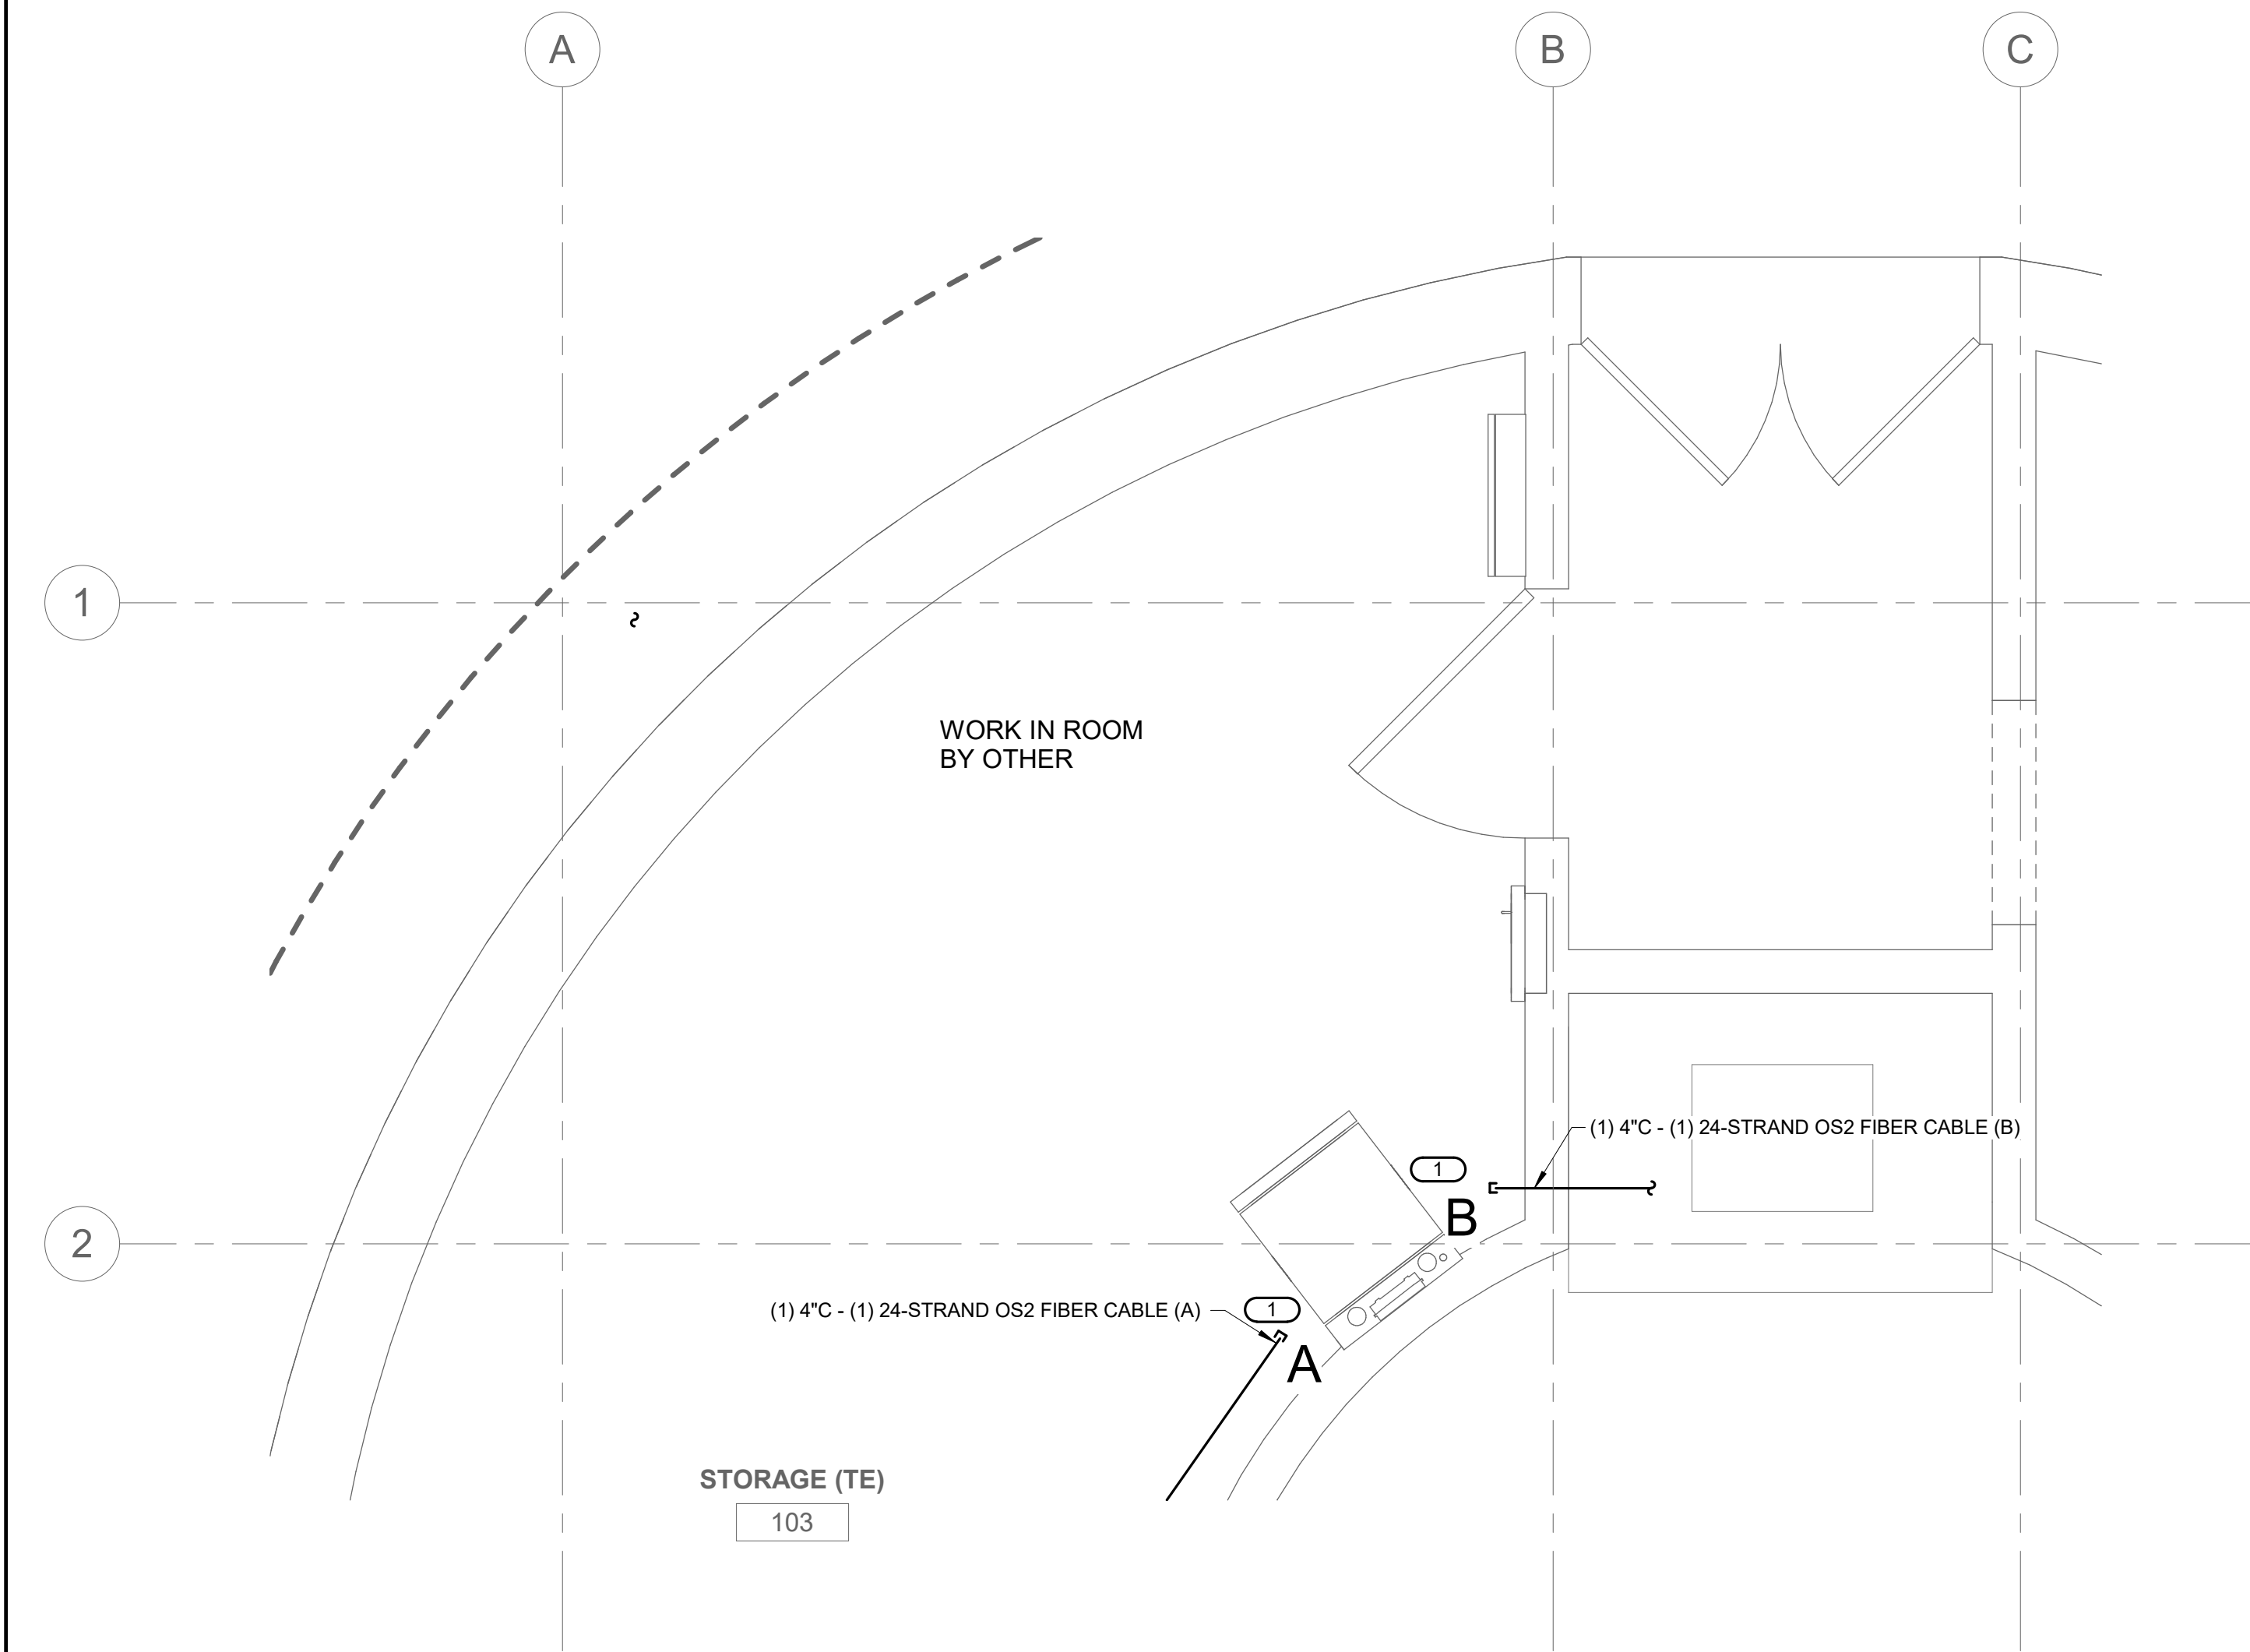

- SHEET NOTES:**
1. REFER TO SITEPLAN TS001 FOR ADDITIONAL INFORMATION.
 2. REFER TO TS00 AND TS01 FOR CAMPUS OPTICAL FIBER CABLE RISER DIAGRAMS.
 3. REFER TO 27400 FOR HANDHOLE DETAIL.
 4. NEW BACKBONE OPTICAL FIBER CABLES SHALL BE INDOOR/OUTDOOR TYPE.
 5. ALL BACKBONE OPTICAL FIBER CABLE PATHWAYS SHALL BE NEW. DO NOT RE-USE EXISTING BACKBONE CABLE PATHWAYS FOR NEW BACKBONE CABLES.
 6. TRANSITION PVC CONDUITS TO GRC IN CRAWL SPACE OR EXPOSED EXTERIOR LOCATIONS. TRANSITION TO EMT CONDUITS AT INTERIOR OF BUILDING. SEAL ALL PENETRATIONS TO MAINTAIN FIRE-RATINGS OF WALL, CEILING AND FLOORS.
- KEY NOTES: (#)**
1. PROVIDE PULLBOX ON EXTERIOR WALL AT HEIGHT ABOVE BASEMENT CEILING. ROUTE CONDUIT UP WALL INTO PULLBOX. PROVIDE PENETRATION THRU WALL AND ROUTE CONDUIT THRU WALL ABOVE CEILING AND OVER TO LOCATION BELOW TR #109A.
 2. PROVIDE PULLBOX ON EXTERIOR WALL AT HEIGHT ABOVE CRAWL SPACE CEILING. ROUTE CONDUIT UP WALL INTO PULLBOX. PROVIDE PENETRATION THRU WALL AND ROUTE CONDUIT THRU WALL INTO CRAWL SPACE AND OVER TO LOCATION BELOW TR #109A.
 3. PROVIDE PENETRATION THRU CEILING AND ROUTE CONDUITS UP INTO TR #109A.

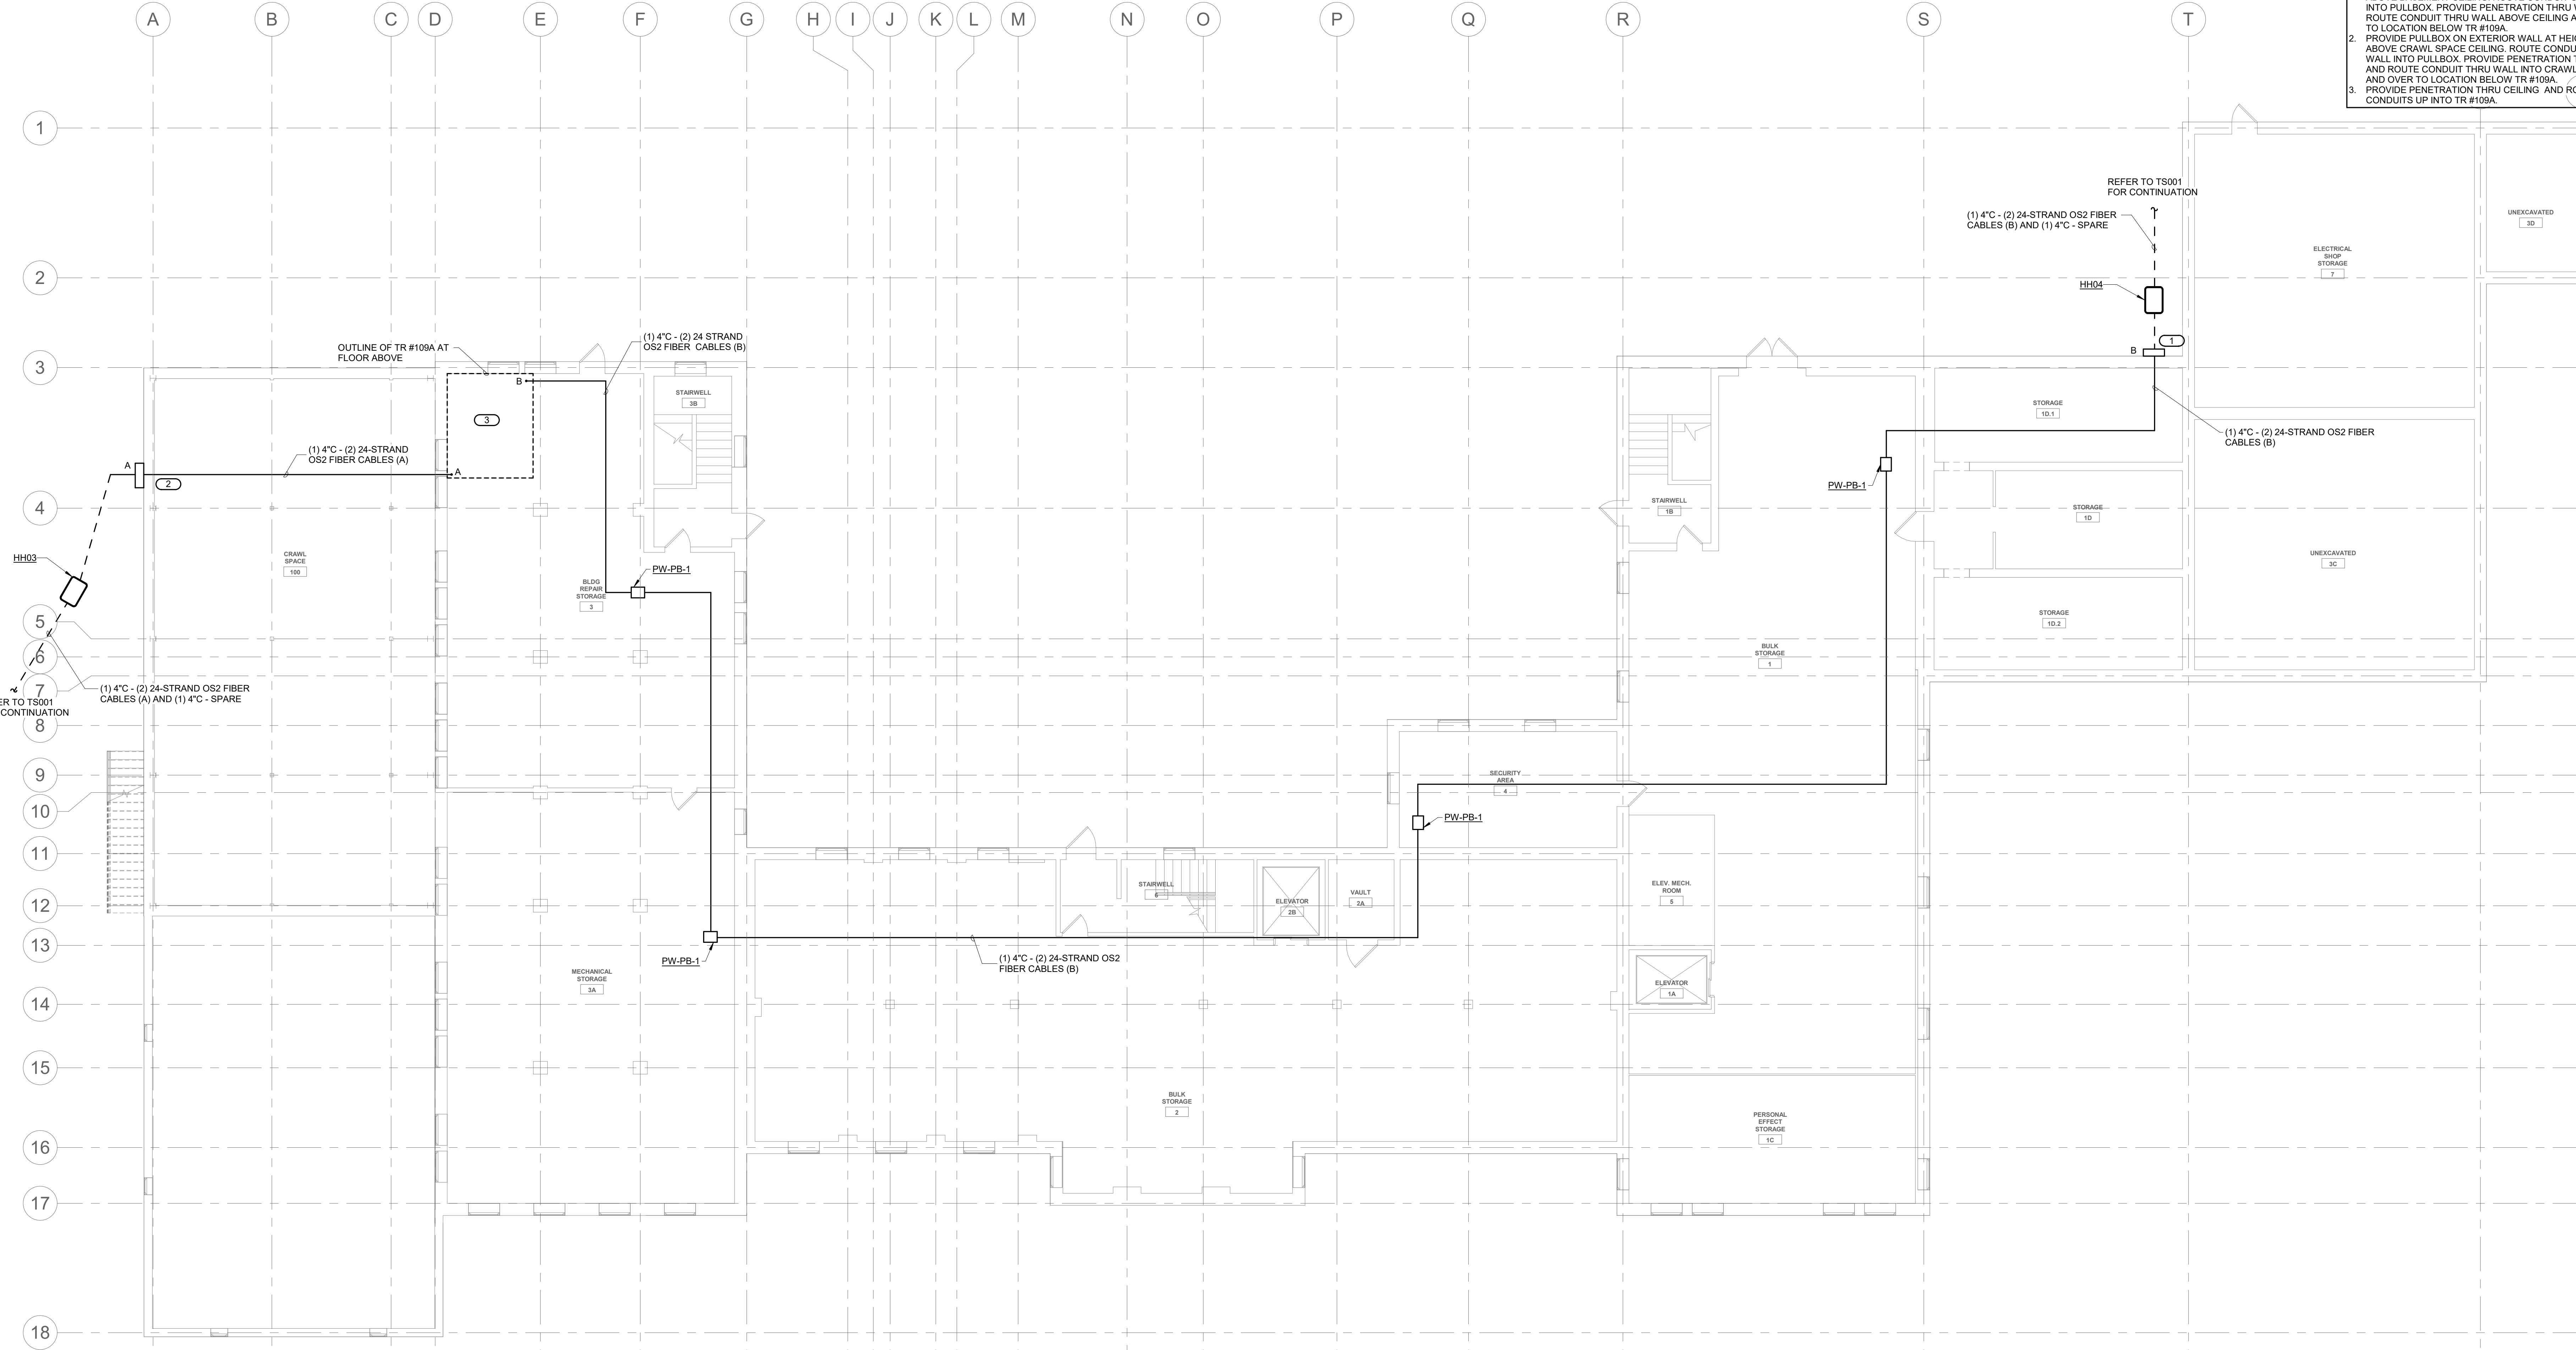


1 BASEMENT PLAN - TECHNOLOGY
1/8" = 1'-0"

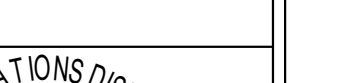		CONSULTANT	ARCHITECT/ENGINEER OF RECORD	STAMP	Office of Construction and Facilities Management VA U.S. Department of Veterans Affairs	Drawing Title BLDG.27 BASEMENT PLAN - TECHNOLOGY	Phase 100% CONSTRUCTION DOCUMENTS	Project Title EHRM INFRASTRUCTURE UPGRADES - HAMPTON	Project Number 509-22-700		
		ENGINEERING DISCIPLINE:  www.imegcorp.com 225 W WASHINGTON STREET SUITE 2700 CHICAGO, IL 60606 P: 312.294.0501 F: 312.294.0003 PROJECT #22010109.00	A/E: SPEES DESIGN BUILD 23830 PACIFIC HIGHWAY S. SUITE 203 KENT, WA 98032  SPEESDESIGNBUILD			Approved:	FULLY SPRINKLERED	Location HAMPTON VA MEDICAL CENTER, HAMPTON, VIRGINIA	Building Number 27		
									Issue Date 05/09/2025	Checked EW	Drawn IMEG
											Drawing Number 27T-200
Revisions:	Date:								642 of 713		

B:\M_360\509-22-700
VAHampton
EHRM\25-700\27T_1.rvt

8/13/2025 1:07:07 PM

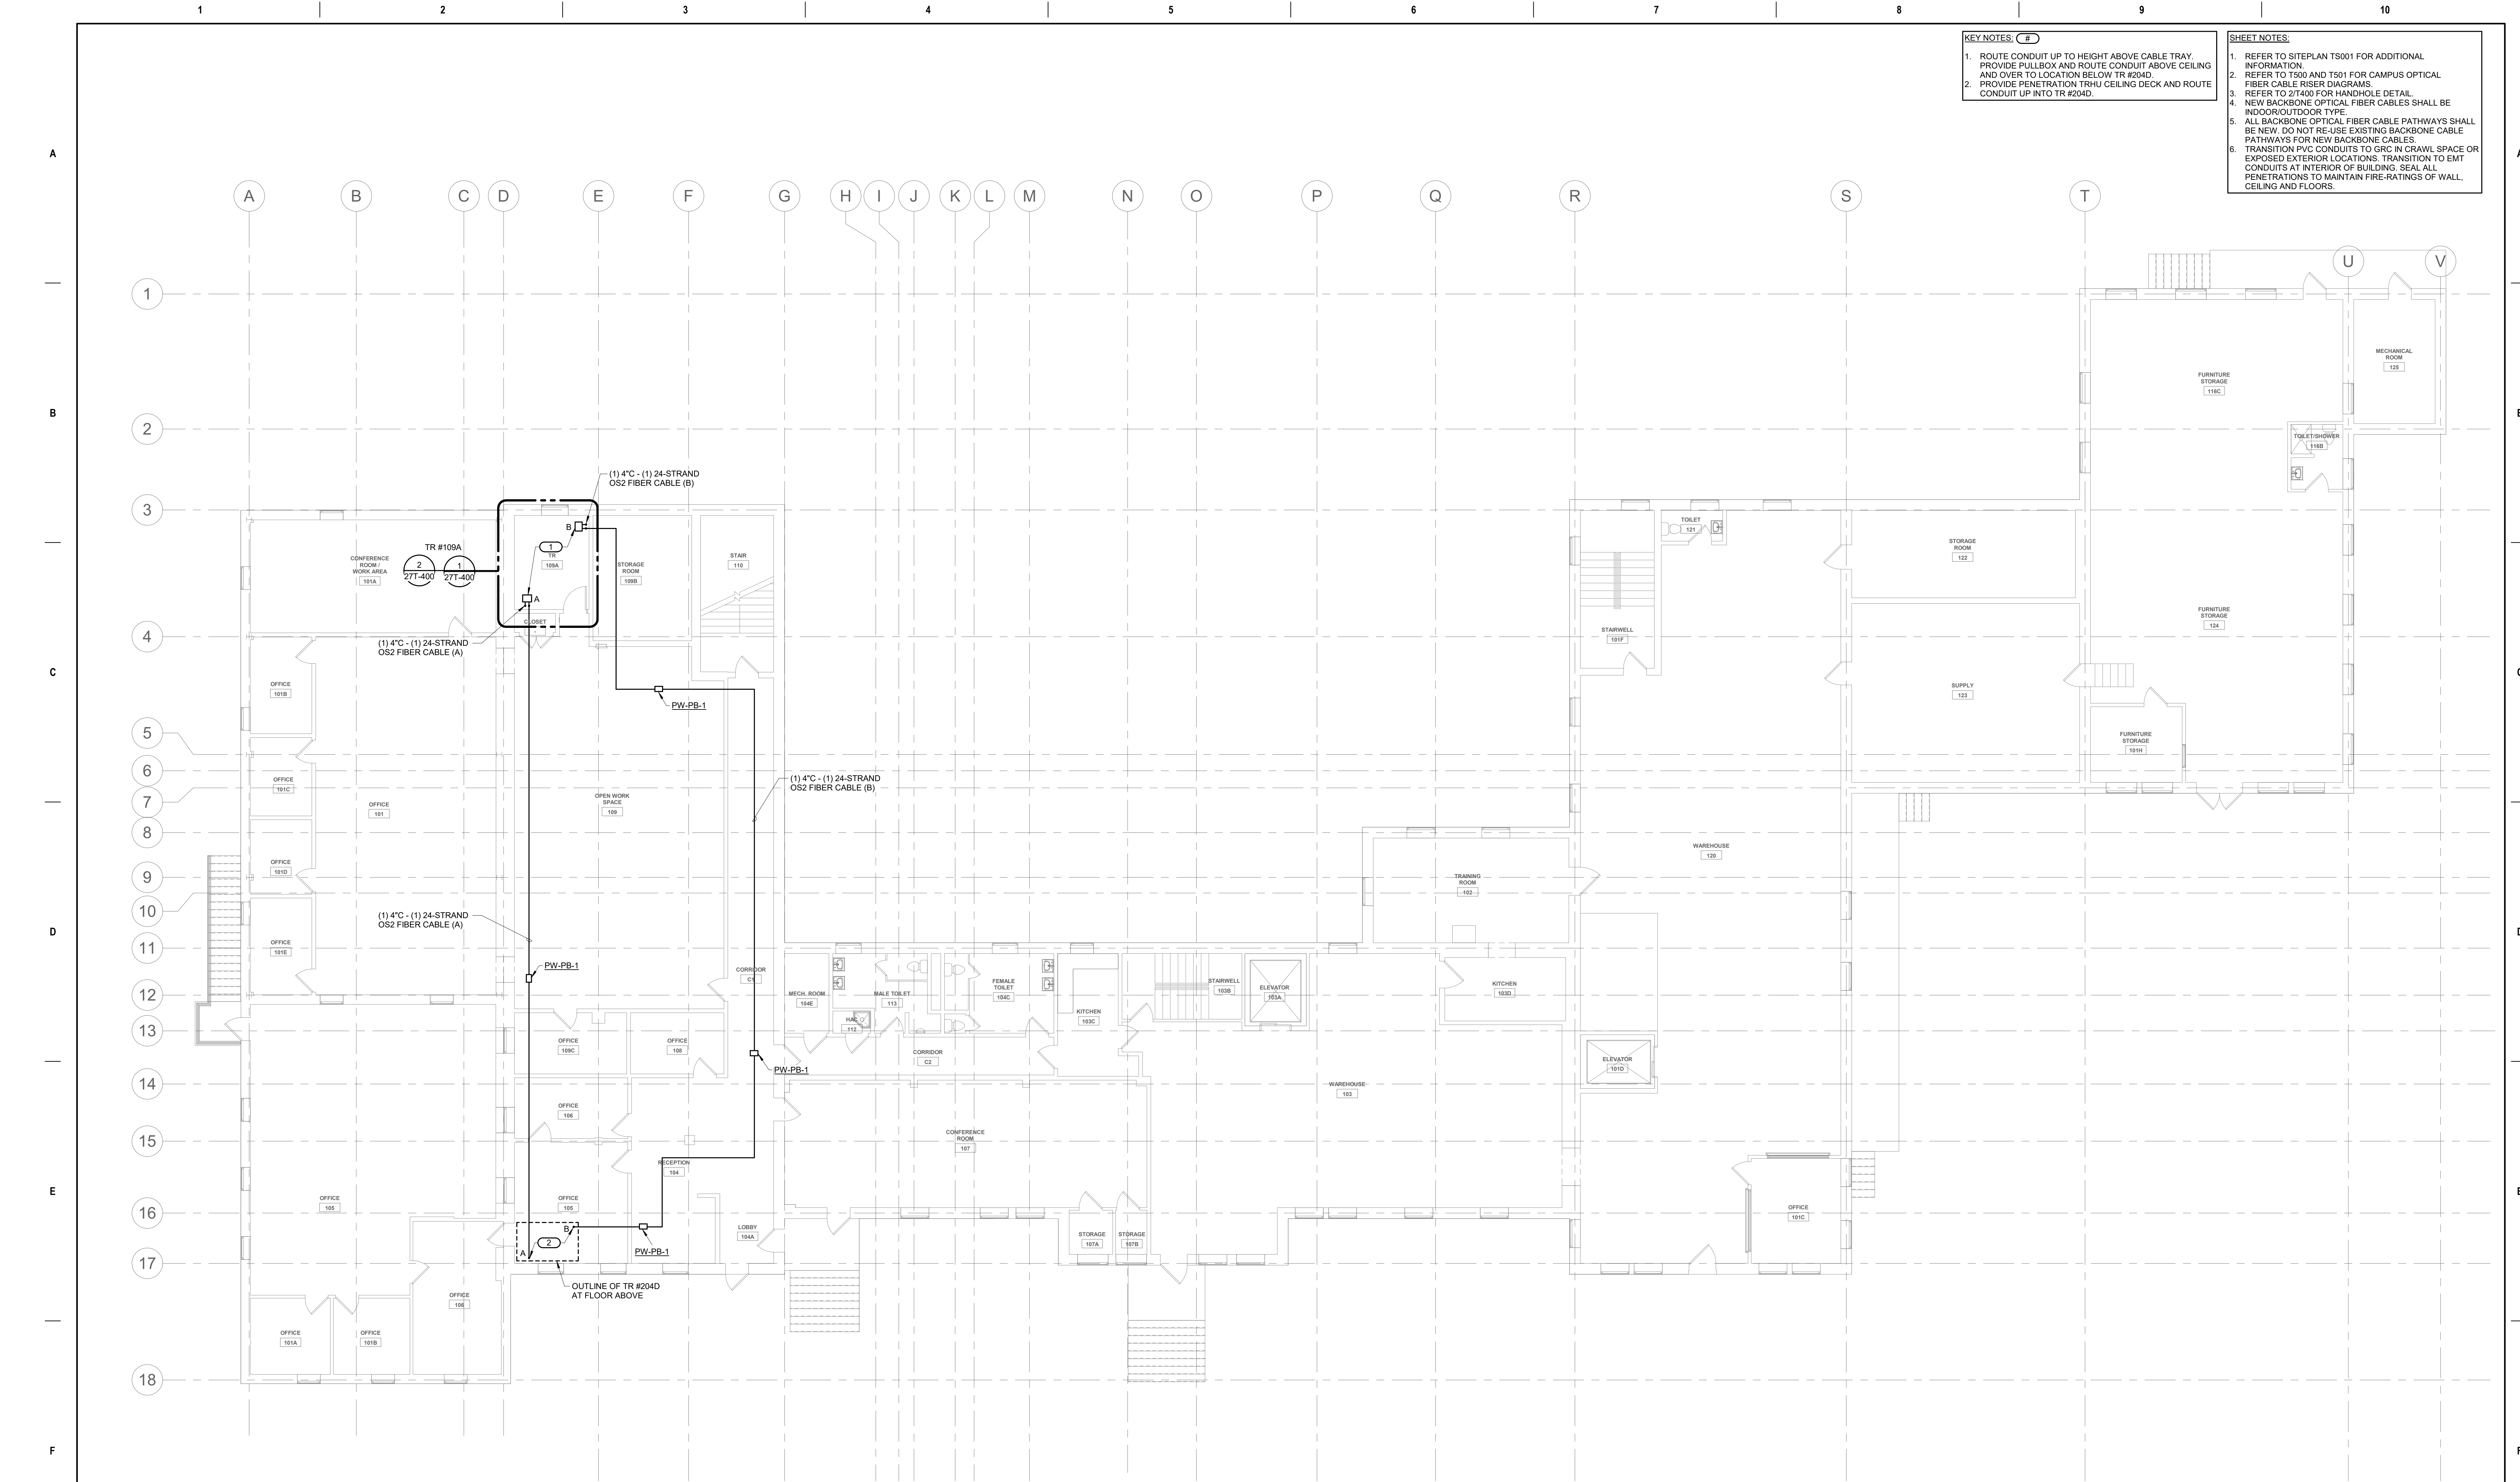

- KEY NOTES:**

 - 1. ROUTE CONDUIT UP TO HEIGHT ABOVE CABLE TRAY. PROVIDE PULLBOX AND ROUTE CONDUIT ABOVE CEILING AND OVER TO LOCATION BELOW TR #204D.
 - 2. PROVIDE PENETRATION TRHU CEILING DECK AND ROUTE CONDUIT UP INTO TR #204D.
- SHEET NOTES:**

 - 1. REFER TO SITEPLAN TS001 FOR ADDITIONAL INFORMATION.
 - 2. REFER TO T500 AND T501 FOR CAMPUS OPTICAL FIBER CABLE RISER DIAGRAMS.
 - 3. REFER TO 27400 FOR HANDHOLE DETAIL.
 - 4. NEW BACKBONE OPTICAL FIBER CABLES SHALL BE INDOOR/OUTDOOR TYPE.
 - 5. ALL BACKBONE OPTICAL FIBER CABLE PATHWAYS SHALL BE NEW. DO NOT RE-USE EXISTING BACKBONE CABLE PATHWAYS FOR NEW BACKBONE CABLES.
 - 6. TRANSITION PVC CONDUITS TO GRC IN CRAWL SPACE OR EXPOSED EXTERIOR LOCATIONS. TRANSITION TO EMT CONDUITS AT INTERIOR OF BUILDING. SEAL ALL PENETRATIONS TO MAINTAIN FIRE-RATINGS OF WALL, CEILING AND FLOORS.


1

LEVEL 01 PLAN - TECHNOLOGY

1/8" = 1'-0"


Revisions: Date:	CONSULTANT ENGINEERING DISCIPLINE:  225 W WASHINGTON STREET SUITE 2700 CHICAGO, IL 60609 P: 312.294.0501 F: 312.294.0003 PROJECT #22010109.00	ARCHITECT/ENGINEER OF RECORD A/E: SPEES DESIGN BUILD 23830 PACIFIC HIGHWAY S. SUITE 203 KENT, WA 98032  SPEESDESIGNBUILD	STAMP  REGISTERED COMMUNICATIONS DISTRIBUTION DESIGNER RCDD	Office of Construction and Facilities Management  U.S. Department of Veterans Affairs	Drawing Title BLDG.27 LEVEL 01 PLAN - TECHNOLOGY	Phase 100% CONSTRUCTION DOCUMENTS	Project Title EHRM INFRASTRUCTURE UPGRADES - HAMPTON	Project Number 509-22-700
					Approved:	FULLY SPRINKLERED	Location HAMPTON VA MEDICAL CENTER, HAMPTON, VIRGINIA	Drawing Number 27T-201
							Issue Date 05/09/2025	Checked EW
							Drawn IMEG	643 of 713

- SHEET NOTES:**
1. REFER TO SITEPLAN TS001 FOR ADDITIONAL INFORMATION.
 2. REFER TO TS00 AND TS01 FOR CAMPUS OPTICAL FIBER CABLE RISER DIAGRAMS.
 3. REFER TO 27T400 FOR HANDHOLE DETAIL.
 4. NEW BACKBONE OPTICAL FIBER CABLES SHALL BE INDOOR/OUTDOOR TYPE.
 5. ALL BACKBONE OPTICAL FIBER CABLE PATHWAYS SHALL BE NEW. DO NOT RE-USE EXISTING BACKBONE CABLE PATHWAYS FOR NEW BACKBONE CABLES.
 6. TRANSITION PVC CONDUITS TO GRC IN CRAWL SPACE OR EXPOSED EXTERIOR LOCATIONS. TRANSITION TO EMT CONDUITS AT INTERIOR OF BUILDING. SEAL ALL PENETRATIONS TO MAINTAIN FIRE-RATINGS OF WALL, CEILING AND FLOORS.
- KEY NOTES:** #
1. ROUTE CONDUIT UP TO HEIGHT ABOVE CABLE TRAY.

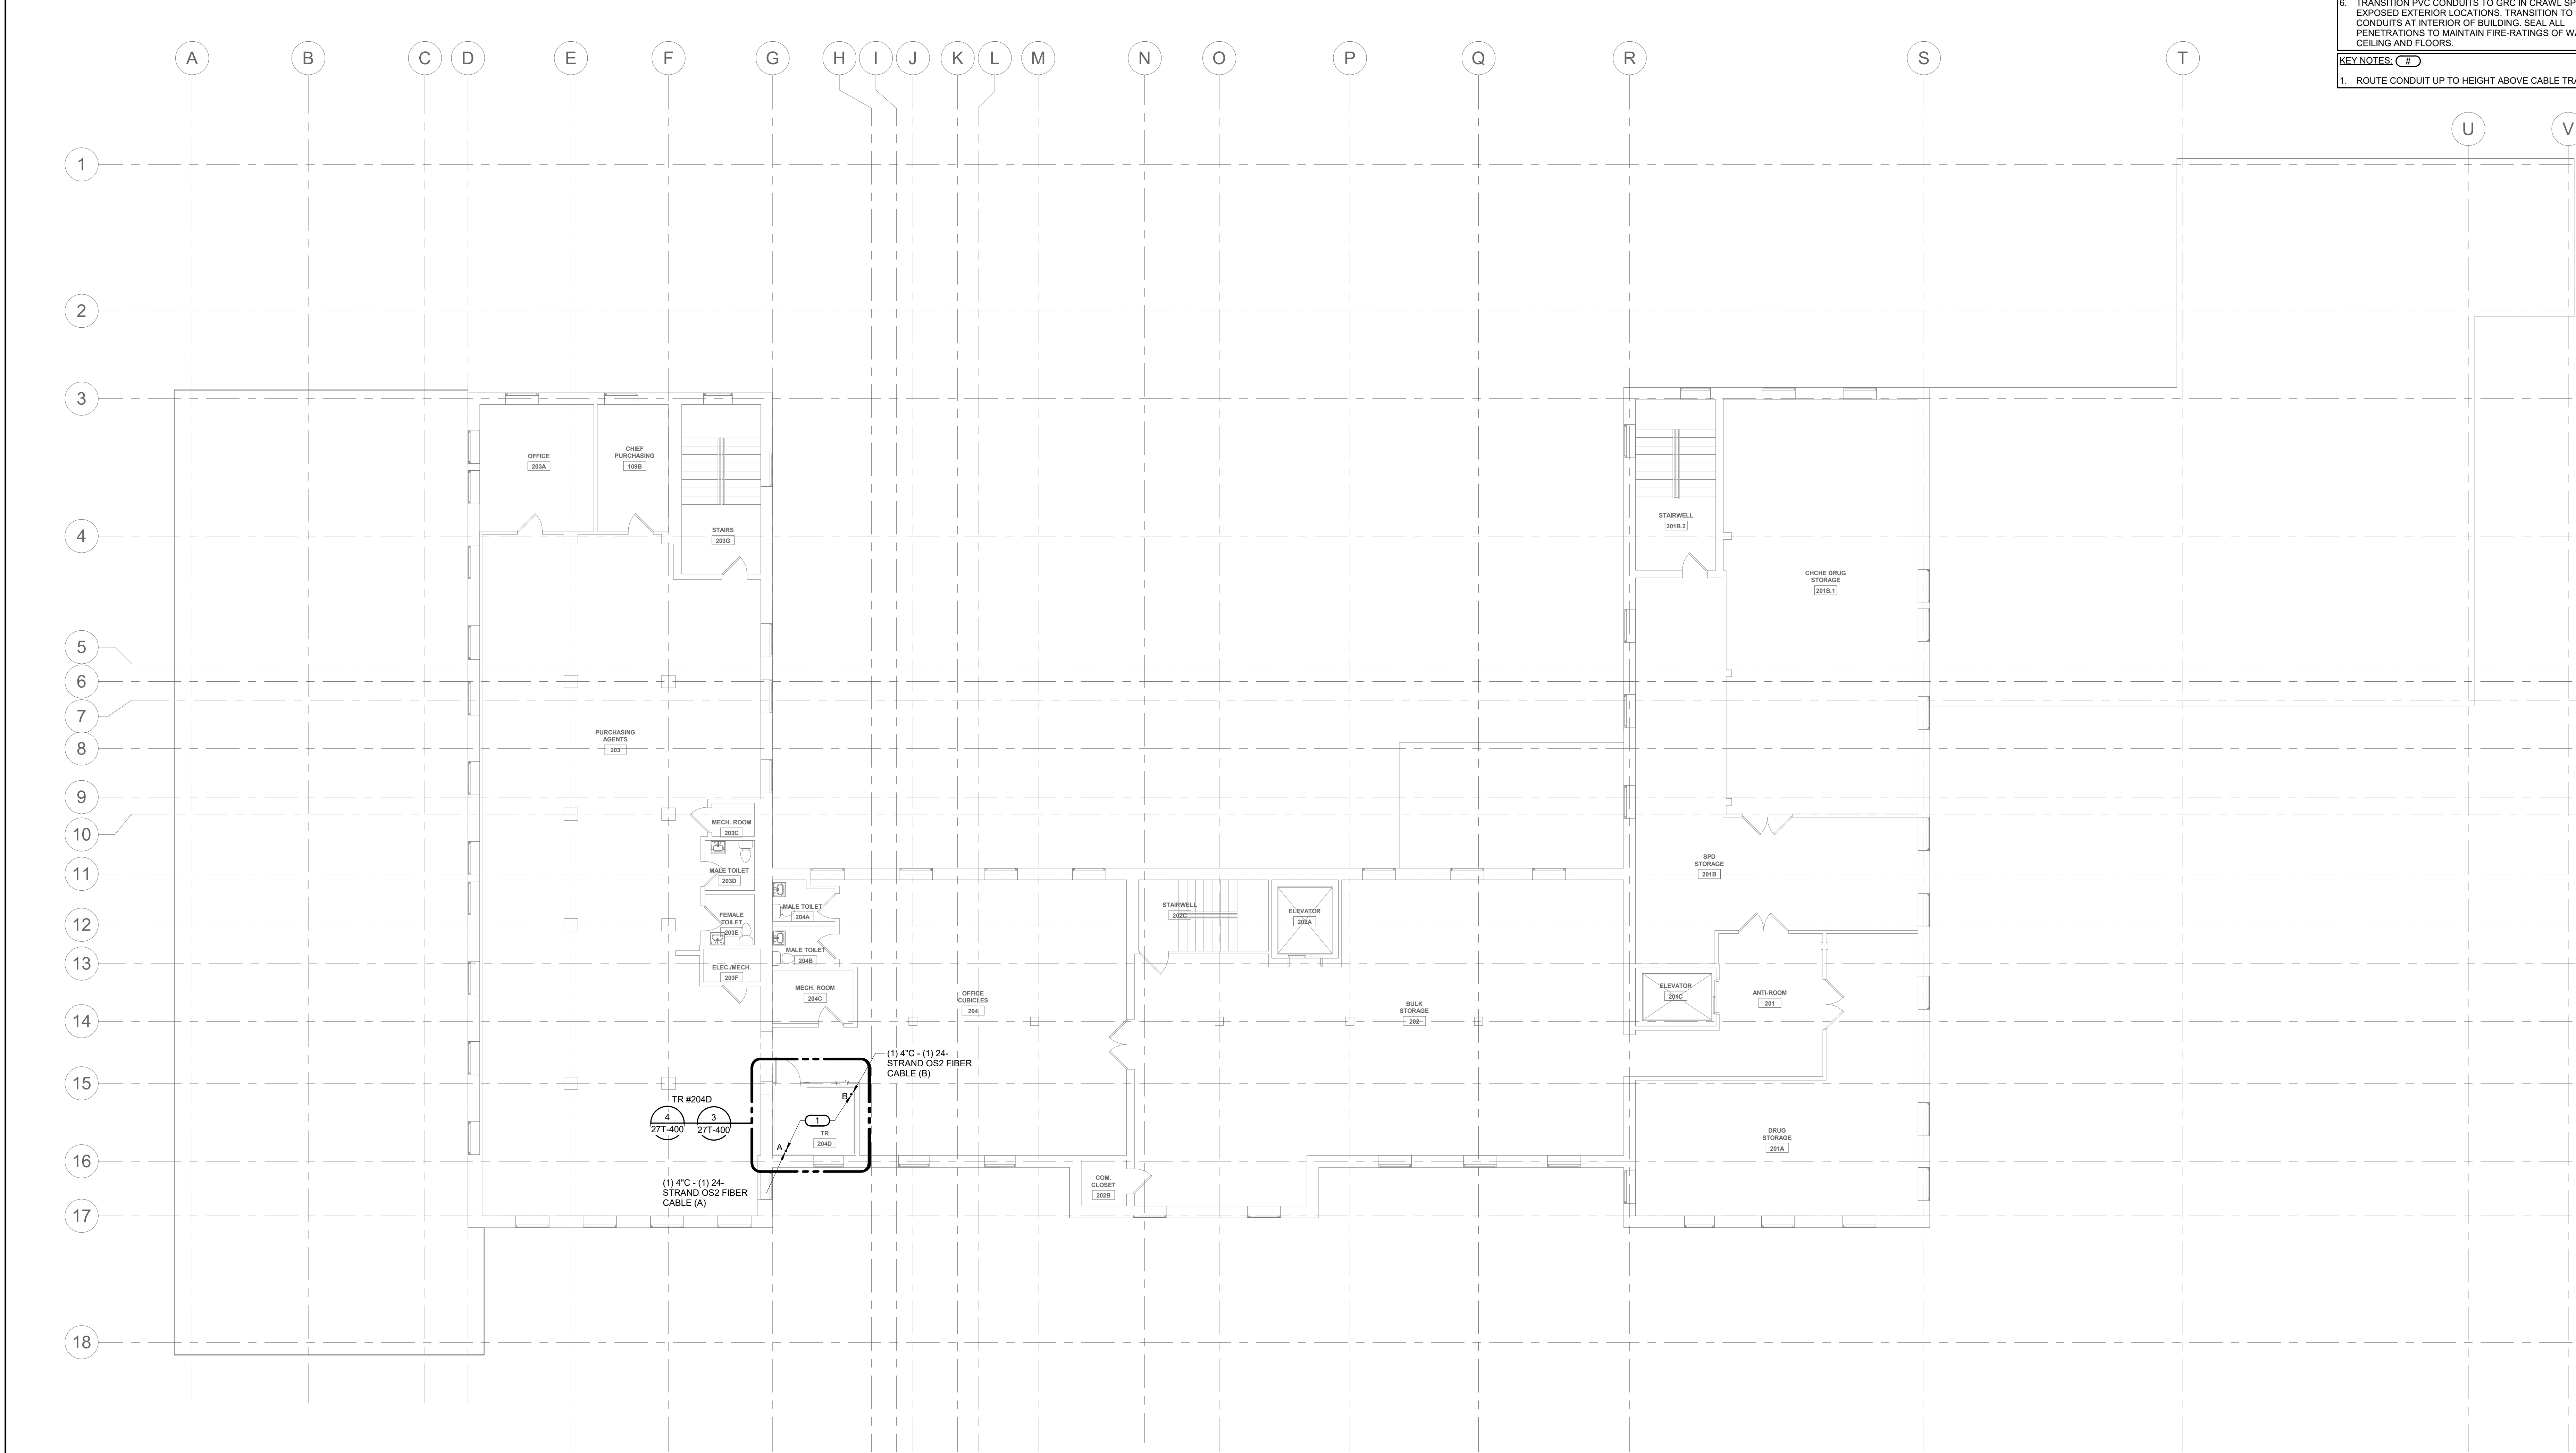

1 LEVEL 02 PLAN - TECHNOLOGY
1/8" = 1'-0"

--	--	

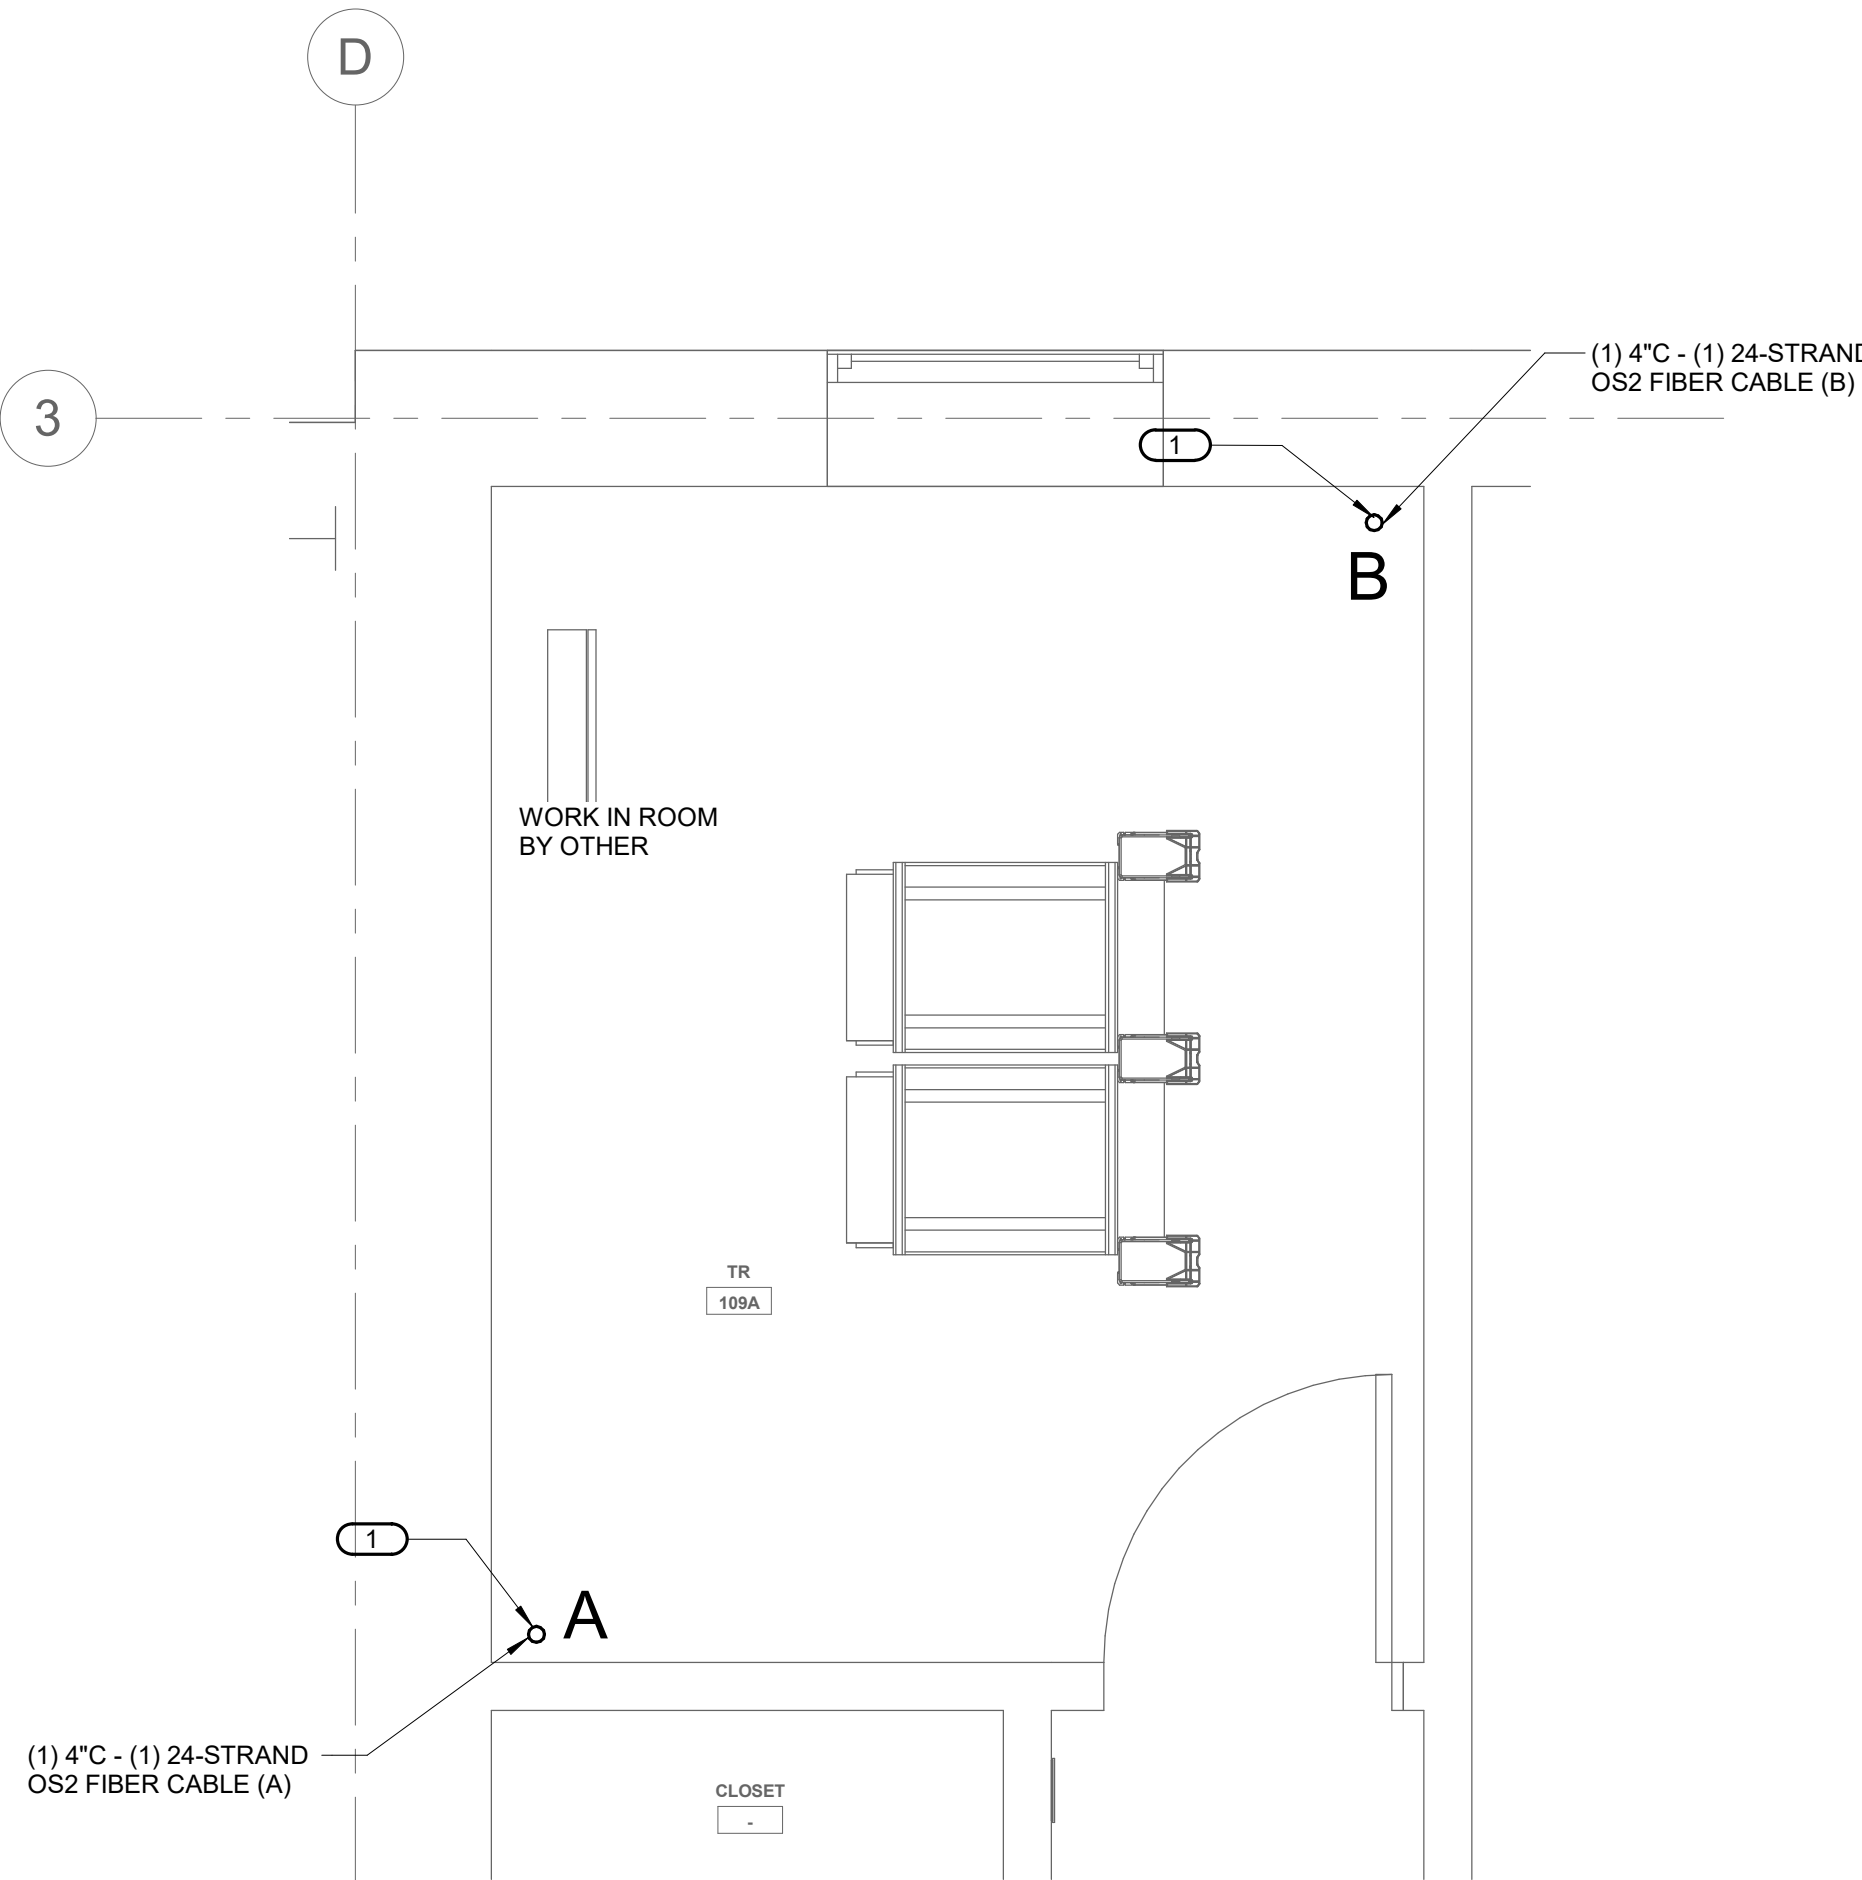


1 TELECOM ROOM ENLARGEMENT TR #109A
1/2" = 1'-0"

NOTES:

1. REFER TO ELECTRICAL DRAWINGS FOR ROOM LAYOUT AND RACK ELEVATIONS.
2. ROUTE OPTICAL FIBER CABLE TO OVERHEAD CABLE TRAY AND TERMINATE IN FIBER DISTRIBUTION CABINET.

KEY NOTES: (B)

1. THROUGH FLOOR/CEILING PENETRATION FOR BACKBONE CONDUIT. CONDUIT SHALL CONTINUE UP TO HEIGHT OF CABLE TRAY. OPTICAL FIBER CABLE CONTINUES ON CABLE TRAY TO RACKS.

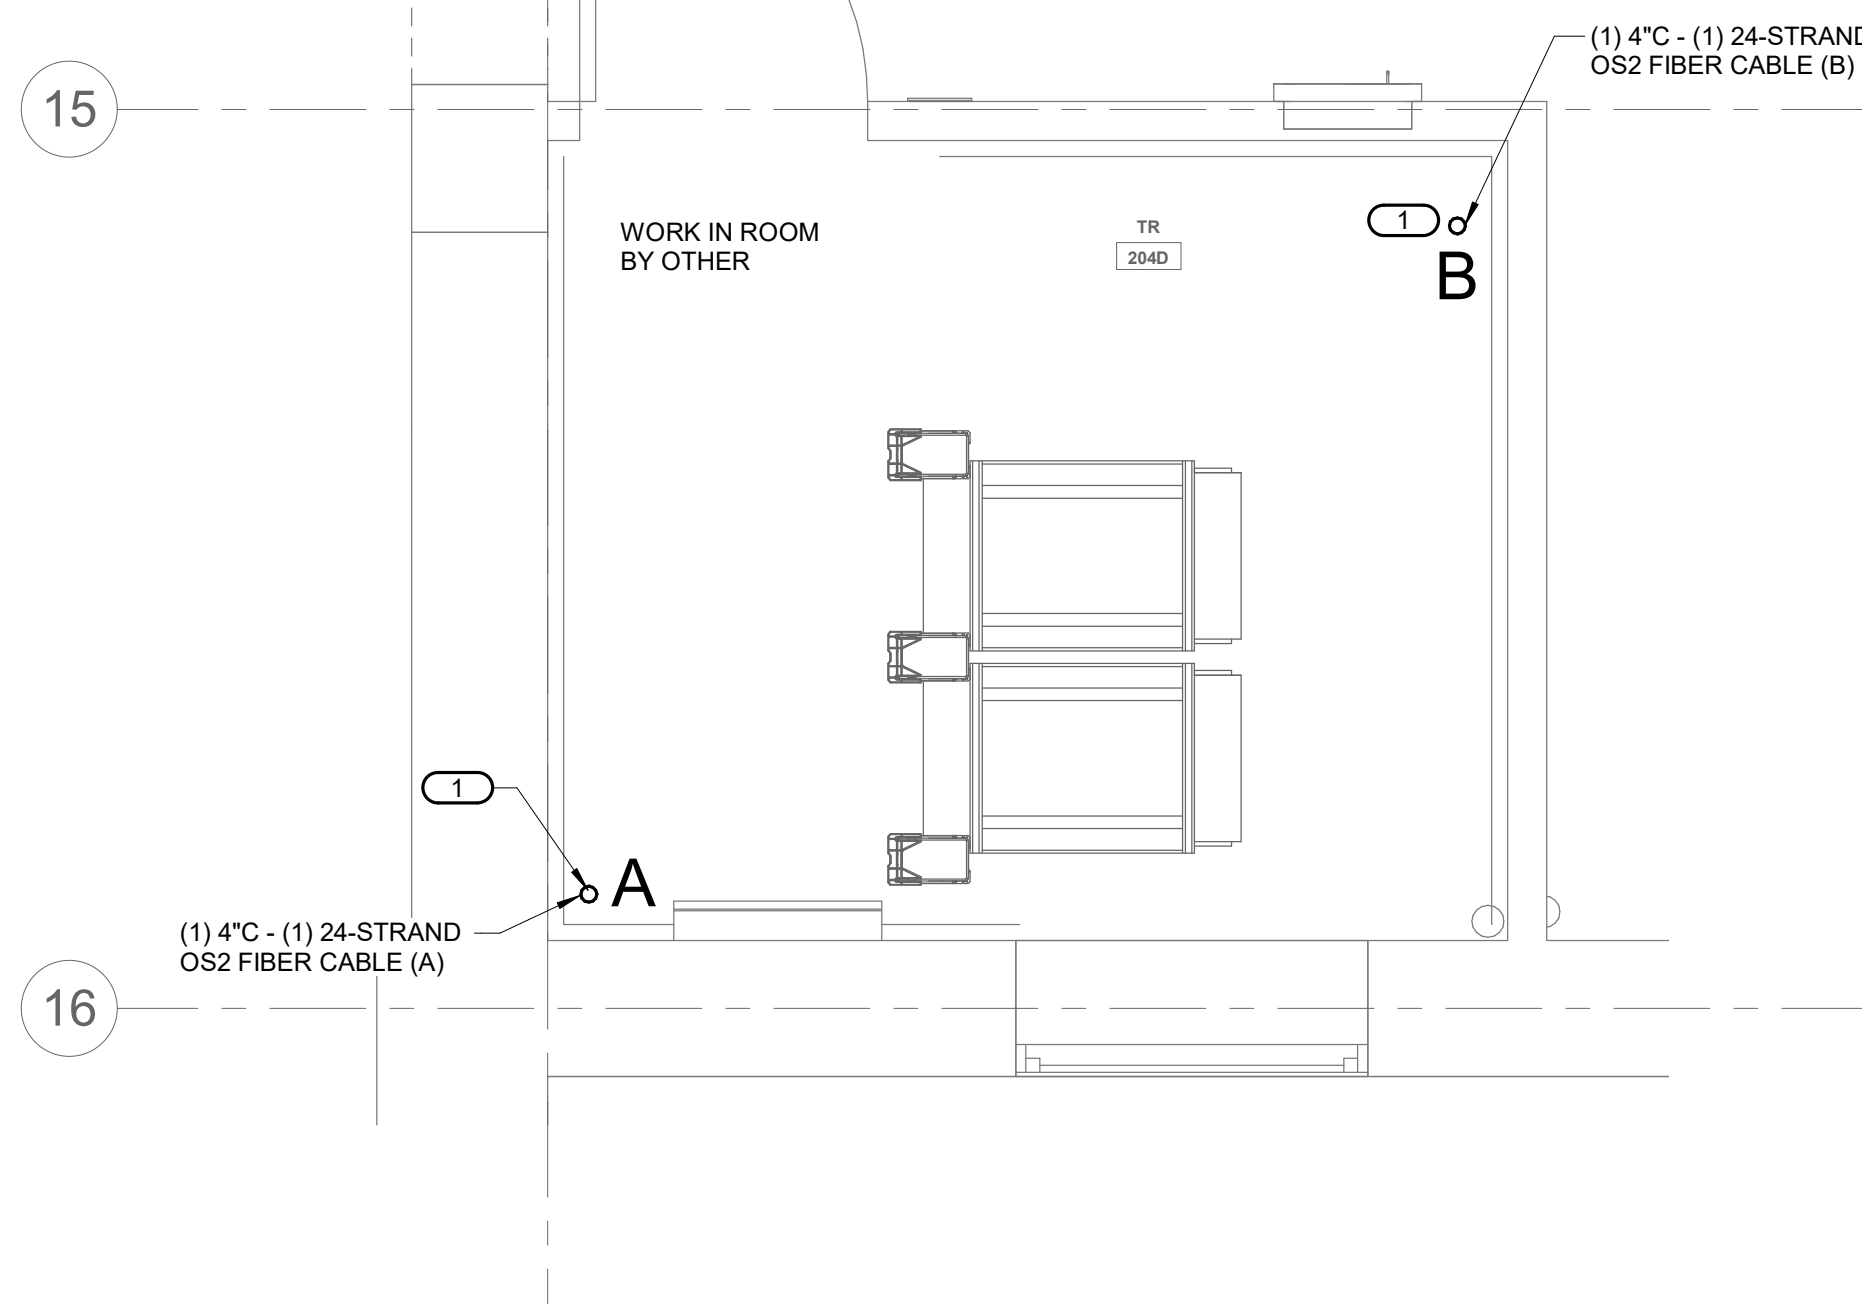


3 TELECOM ROOM ENLARGEMENT TR #204D
1/2" = 1'-0"

NOTES:


1. REFER TO ELECTRICAL DRAWINGS FOR ROOM LAYOUT AND RACK ELEVATIONS.
2. ROUTE OPTICAL FIBER CABLE TO OVERHEAD CABLE TRAY AND TERMINATE IN FIBER DISTRIBUTION CABINET.

KEY NOTES: (B)


1. THROUGH FLOOR/CEILING PENETRATION FOR BACKBONE CONDUIT. CONDUIT SHALL CONTINUE UP TO HEIGHT OF CABLE TRAY. OPTICAL FIBER CABLE CONTINUES ON CABLE TRAY TO RACKS.

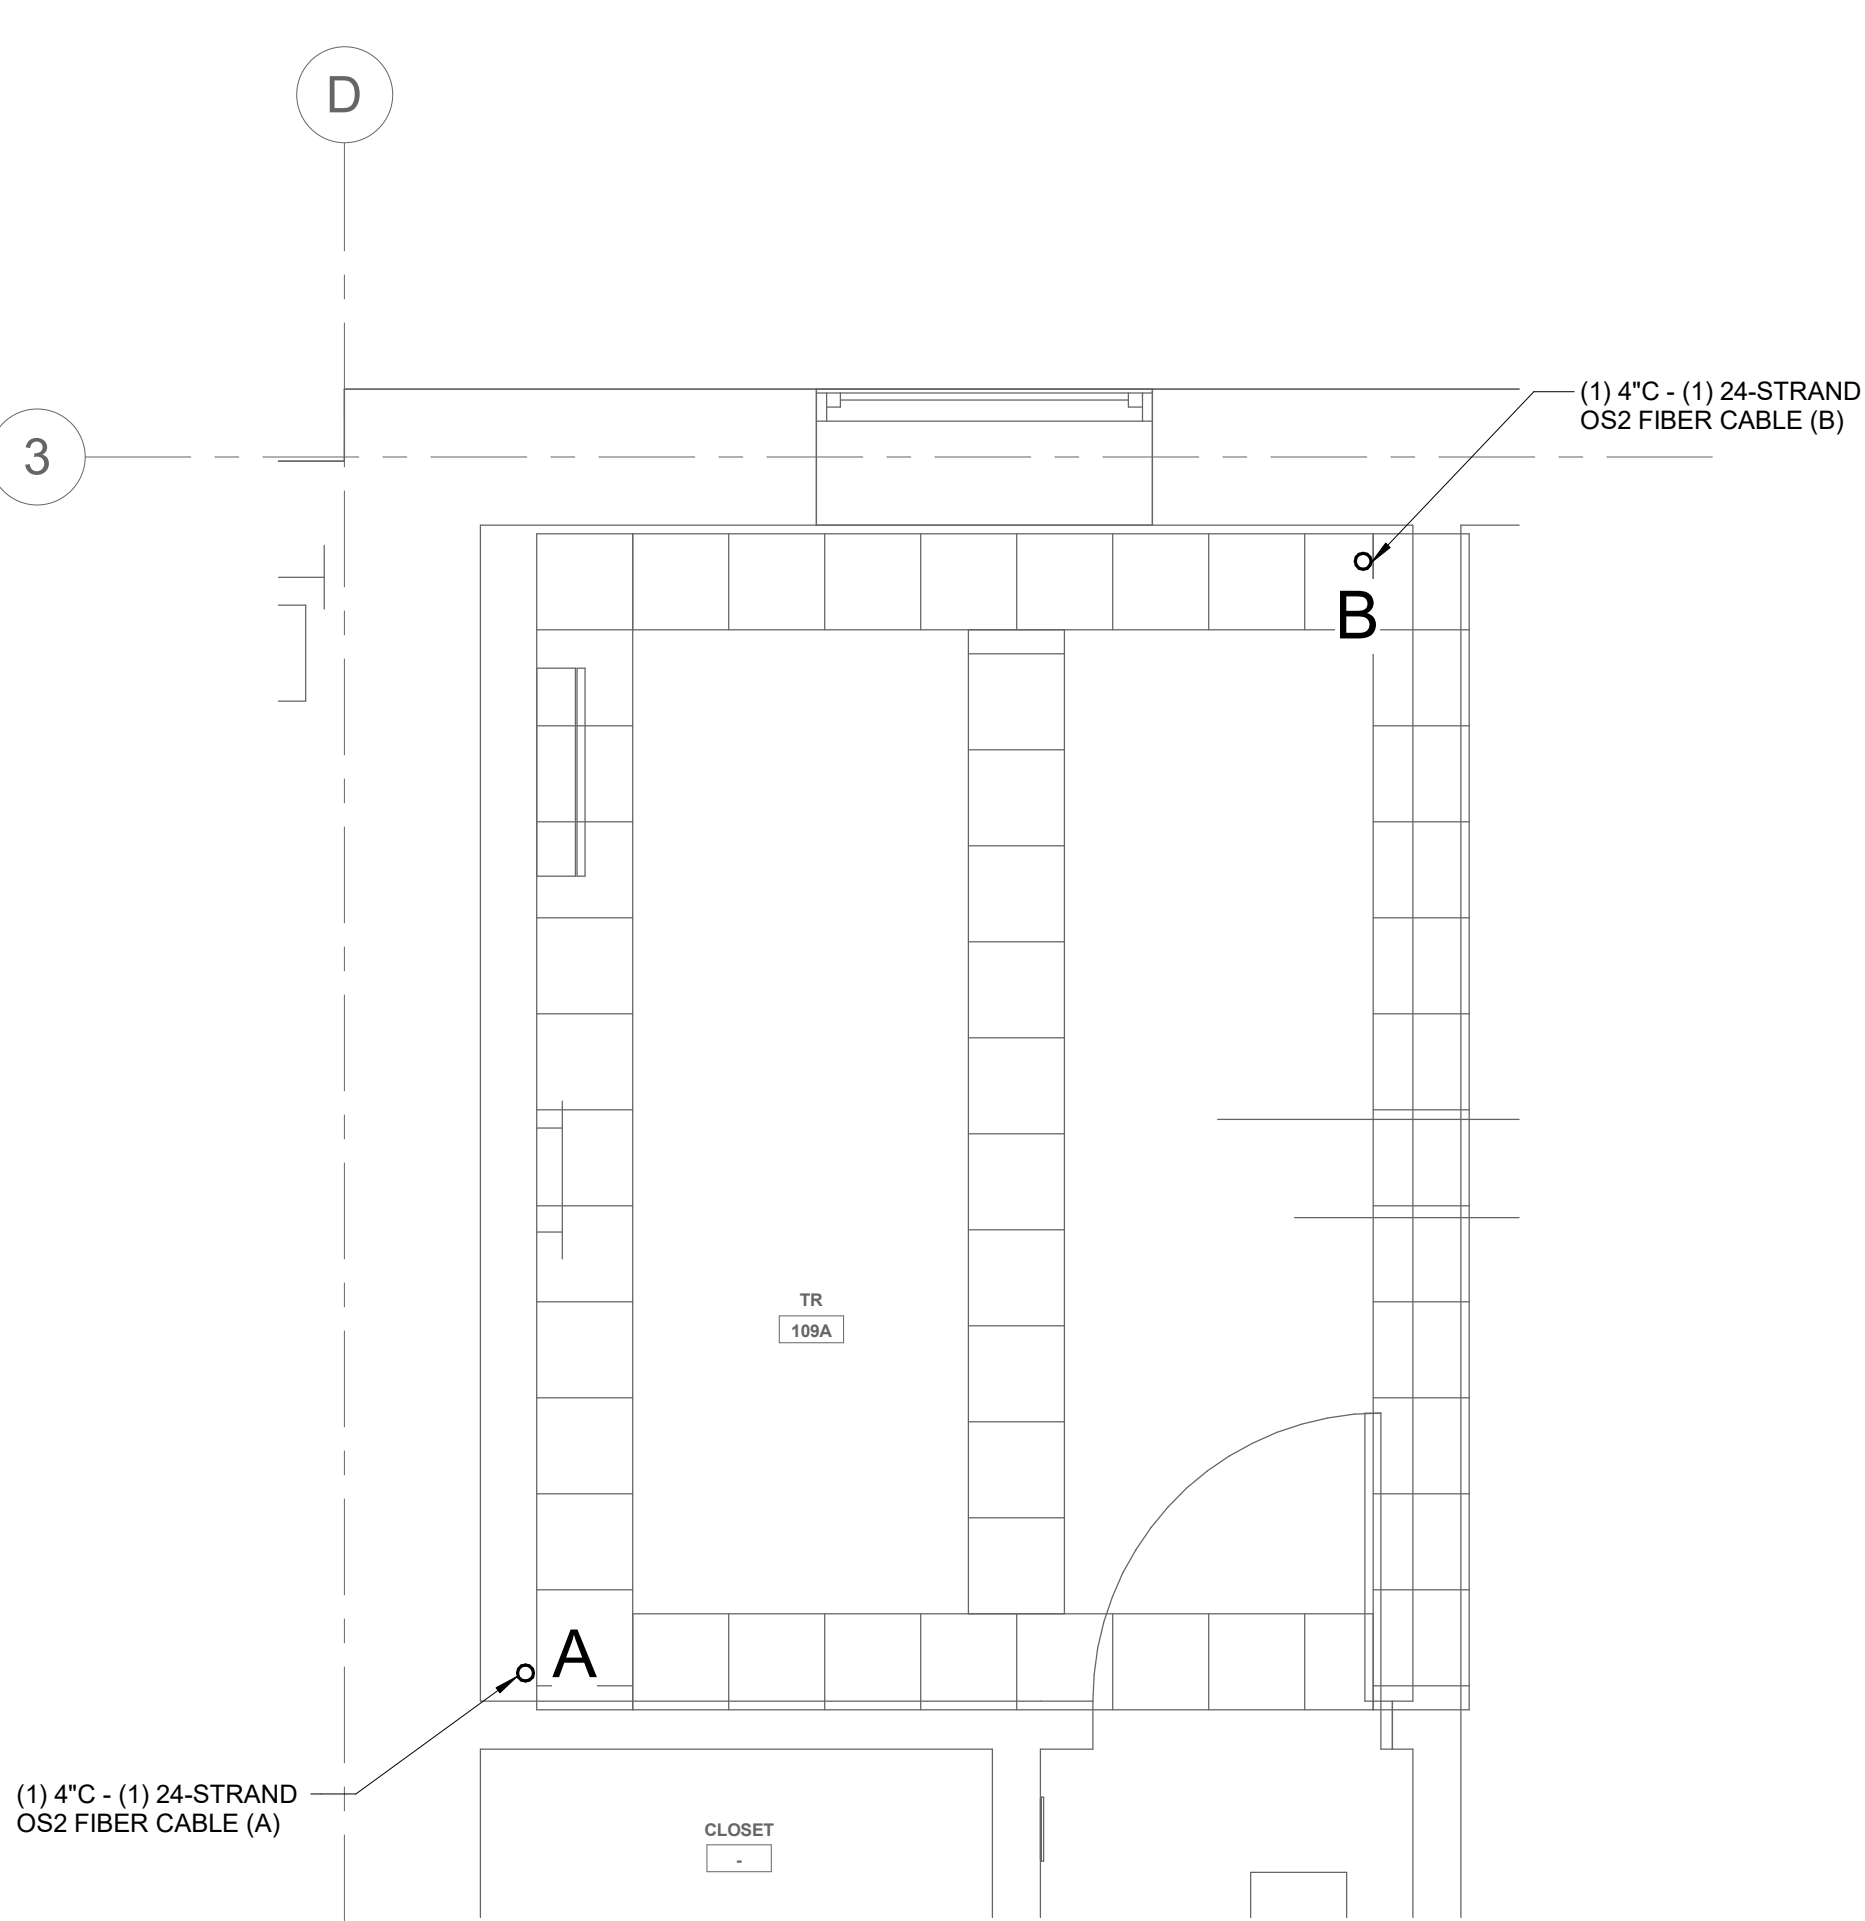

2 TELECOM ROOM PATHWAY TR #109A
1/2" = 1'-0"

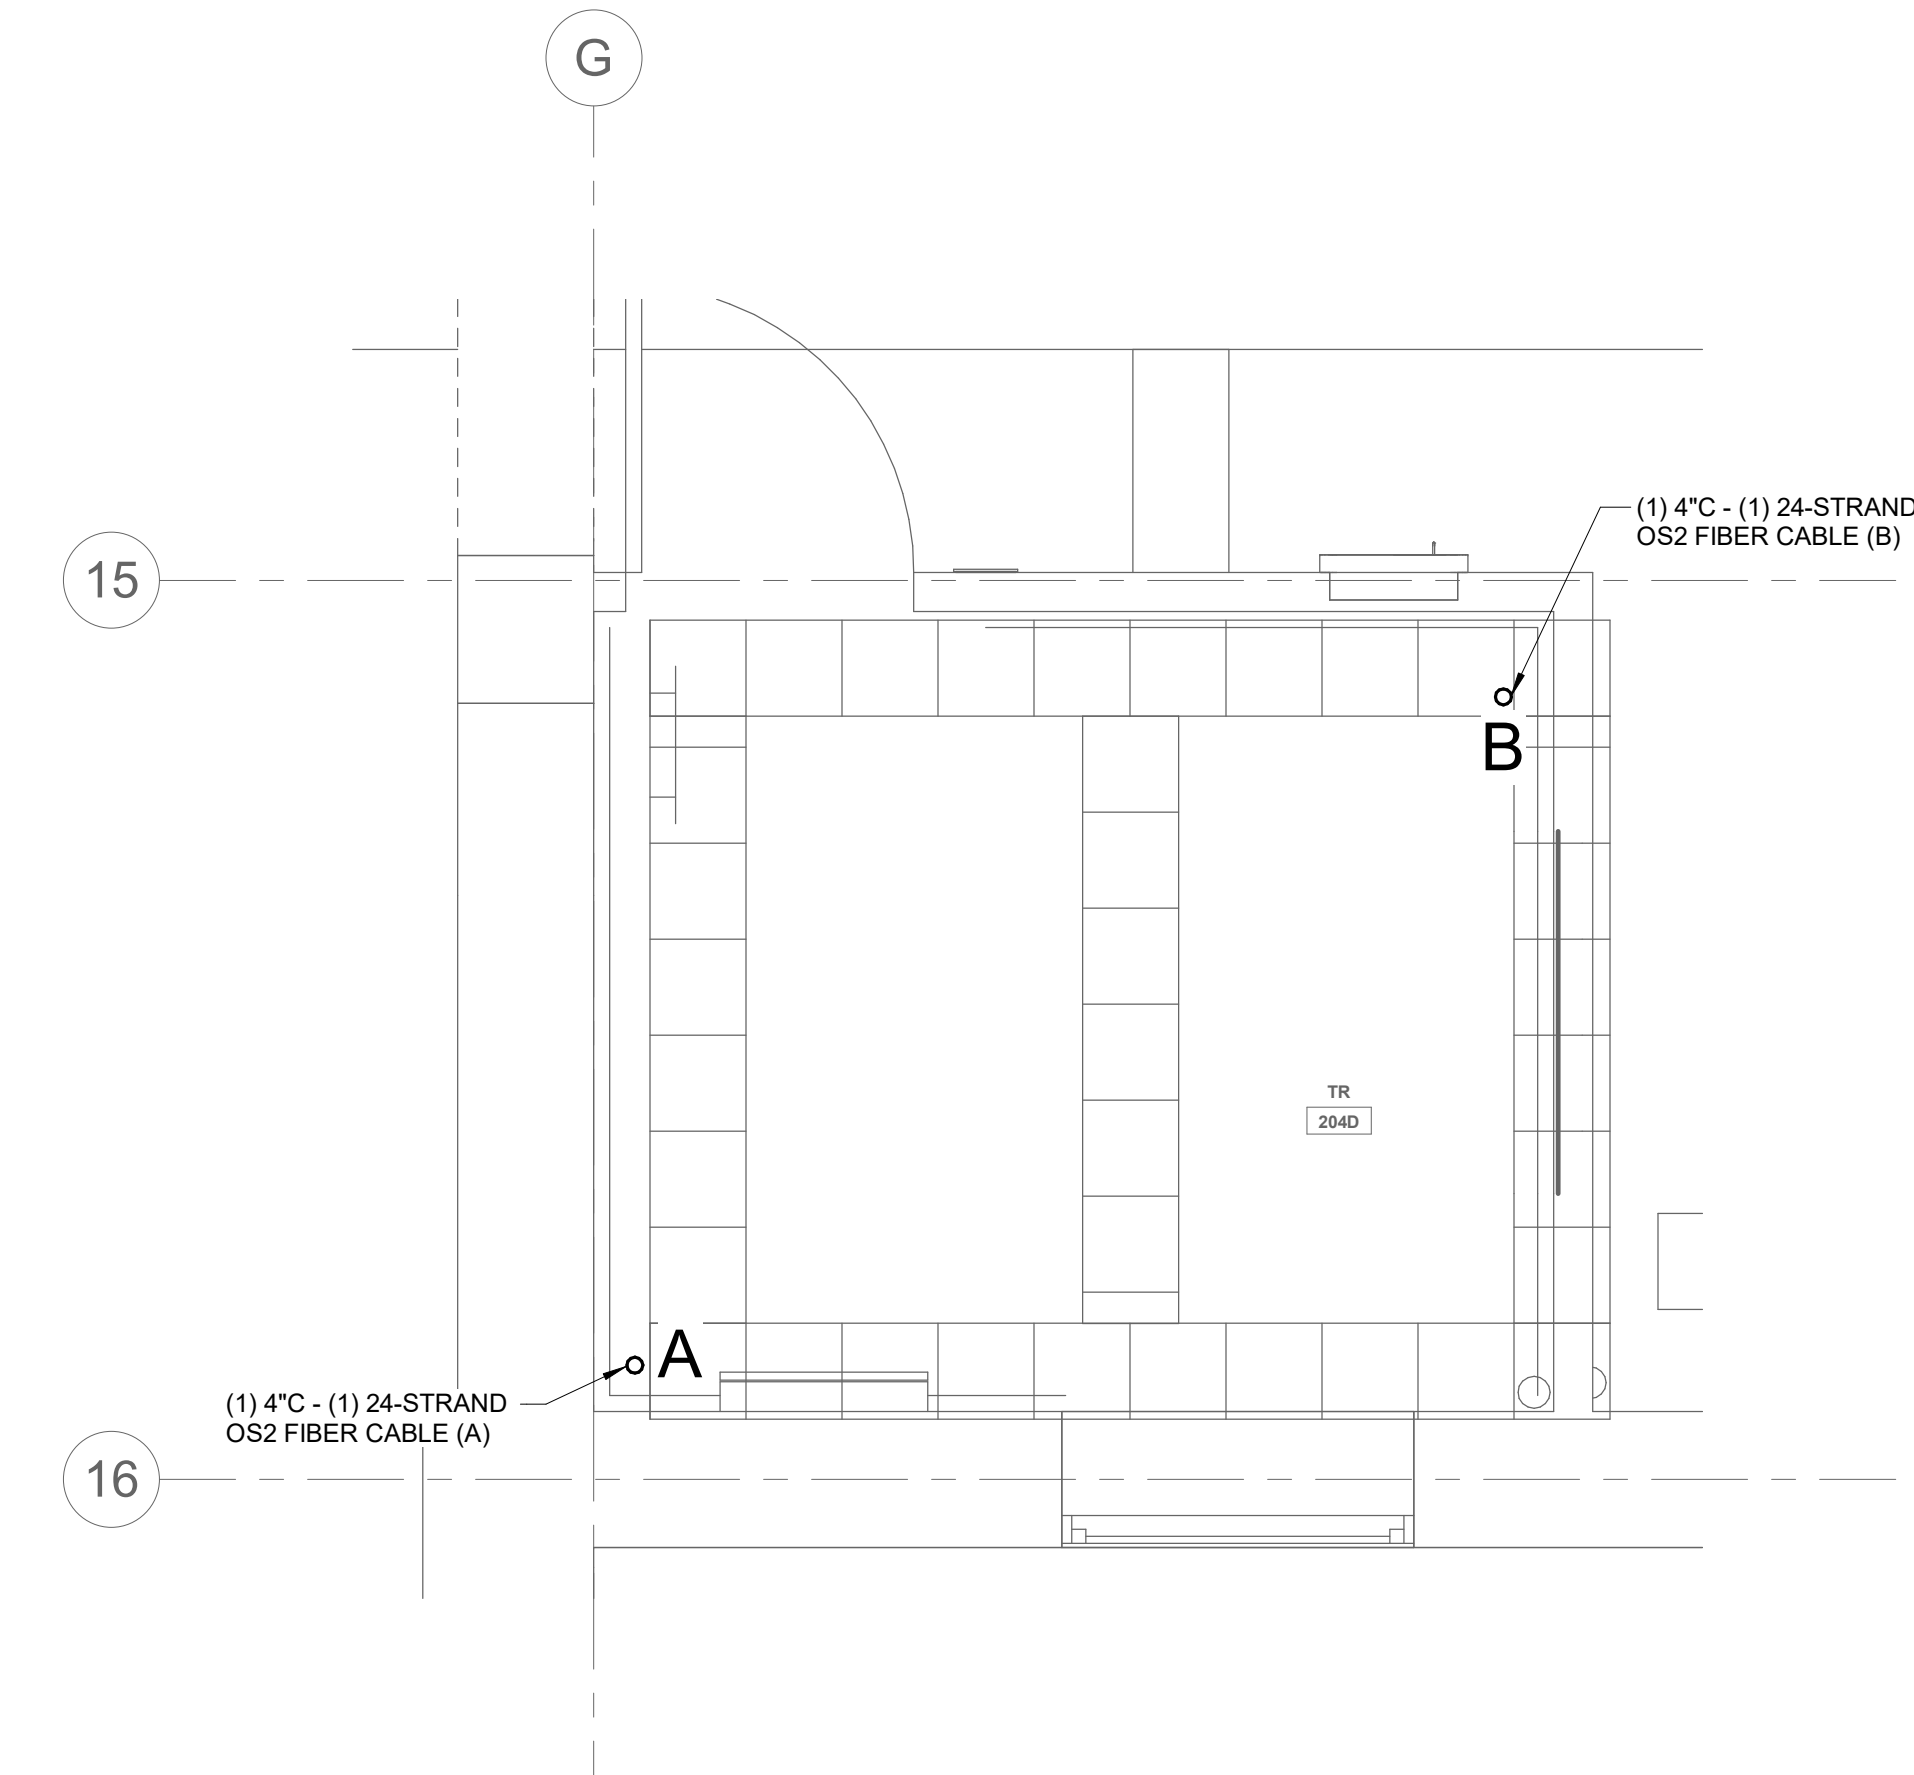

4 TELECOM ROOM PATHWAY TR #204D
1/2" = 1'-0"

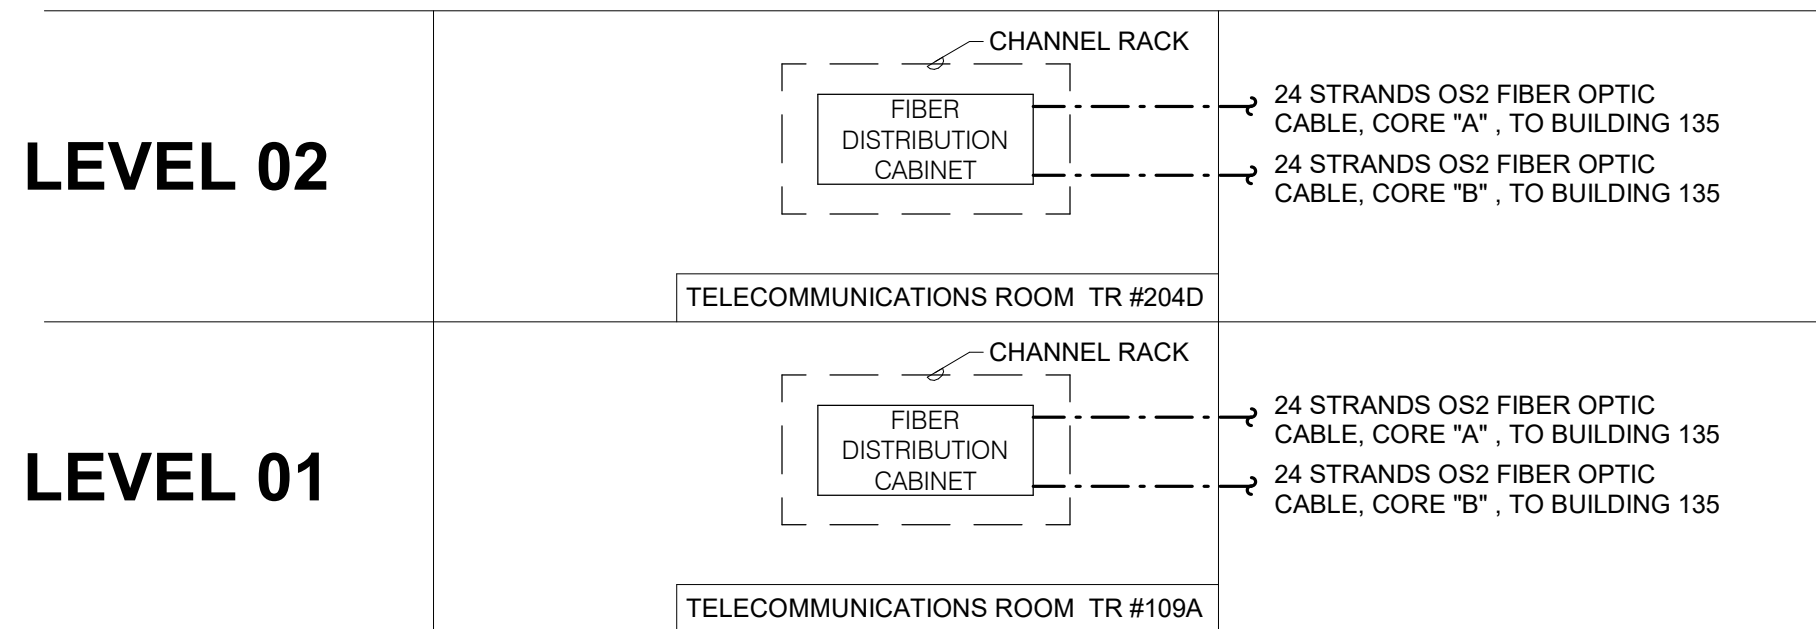


5 FIBER RISER DIAGRAM
NO SCALE

NOTES:

1. THIS RISER IS DIAGRAMMATIC AND MAY NOT SHOW ACTUAL ROUTING OR QUANTITIES OF MATERIALS SHOWN. THIS RISER IS SHOWN FOR CLARIFICATION OF CONNECTION(S) LOCATIONS AND CABLE TYPE. ALL INFORMATION OUTLETS ARE TYPICAL OF THE OUTLETS IN THE AREA SHOWN. REFER TO FLOOR PLANS FOR MORE SPECIFIC ROUTING INFORMATION. REFER TO SPECIFICATIONS FOR ADDITIONAL REQUIREMENTS.
2. REFER TO ELECTRICAL DRAWINGS FOR CHANNEL RACK AND FIBER OPTIC DISTRIBUTION CABINET SPECIFICATIONS


--	--	

- SHEET NOTES:**
1. REFER TO TS001 FOR ADDITIONAL INFORMATION.
 2. REFER TO TS00 AND TS01 FOR CAMPUS OPTICAL FIBER CABLE RISER DIAGRAMS.
 3. REFER TO 27400 FOR HANDHOLE DETAIL.
 4. NEW BACKBONE OPTICAL FIBER CABLES SHALL BE INDOOR/OUTDOOR TYPE.
 5. ALL BACKBONE OPTICAL FIBER CABLE PATHWAYS SHALL BE NEW. DO NOT RE-USE EXISTING BACKBONE CABLE PATHWAYS FOR NEW BACKBONE CABLES.
 6. TRANSITION PVC CONDUITS TO GRC IN CRAWL SPACE OR EXPOSED EXTERIOR LOCATIONS. TRANSITION TO EMT CONDUITS AT INTERIOR OF BUILDING. SEAL ALL PENETRATIONS TO MAINTAIN FIRE-RATINGS OF WALL, CEILING AND FLOORS.
- KEY NOTES:**
1. PROVIDE PULLBOX ON EXTERIOR WALL AT HEIGHT ABOVE FINISHED CEILING. ROUTE CONDUIT UP WALL INTO PULLBOX. PROVIDE PENETRATION THRU WALL AND ROUTE CONDUIT THRU WALL ABOVE CEILING AND INTO TR #103B.1a.
 2. PROVIDE PULLBOX ON EXTERIOR WALL ABOVE CABLE TRAY HEIGHT IN TR #103B.1a ROUTE CONDUIT UP WALL INTO PULLBOX. PROVIDE PENETRATION THRU WALL AND STUB CONDUIT ABOVE CABLE TRAY.

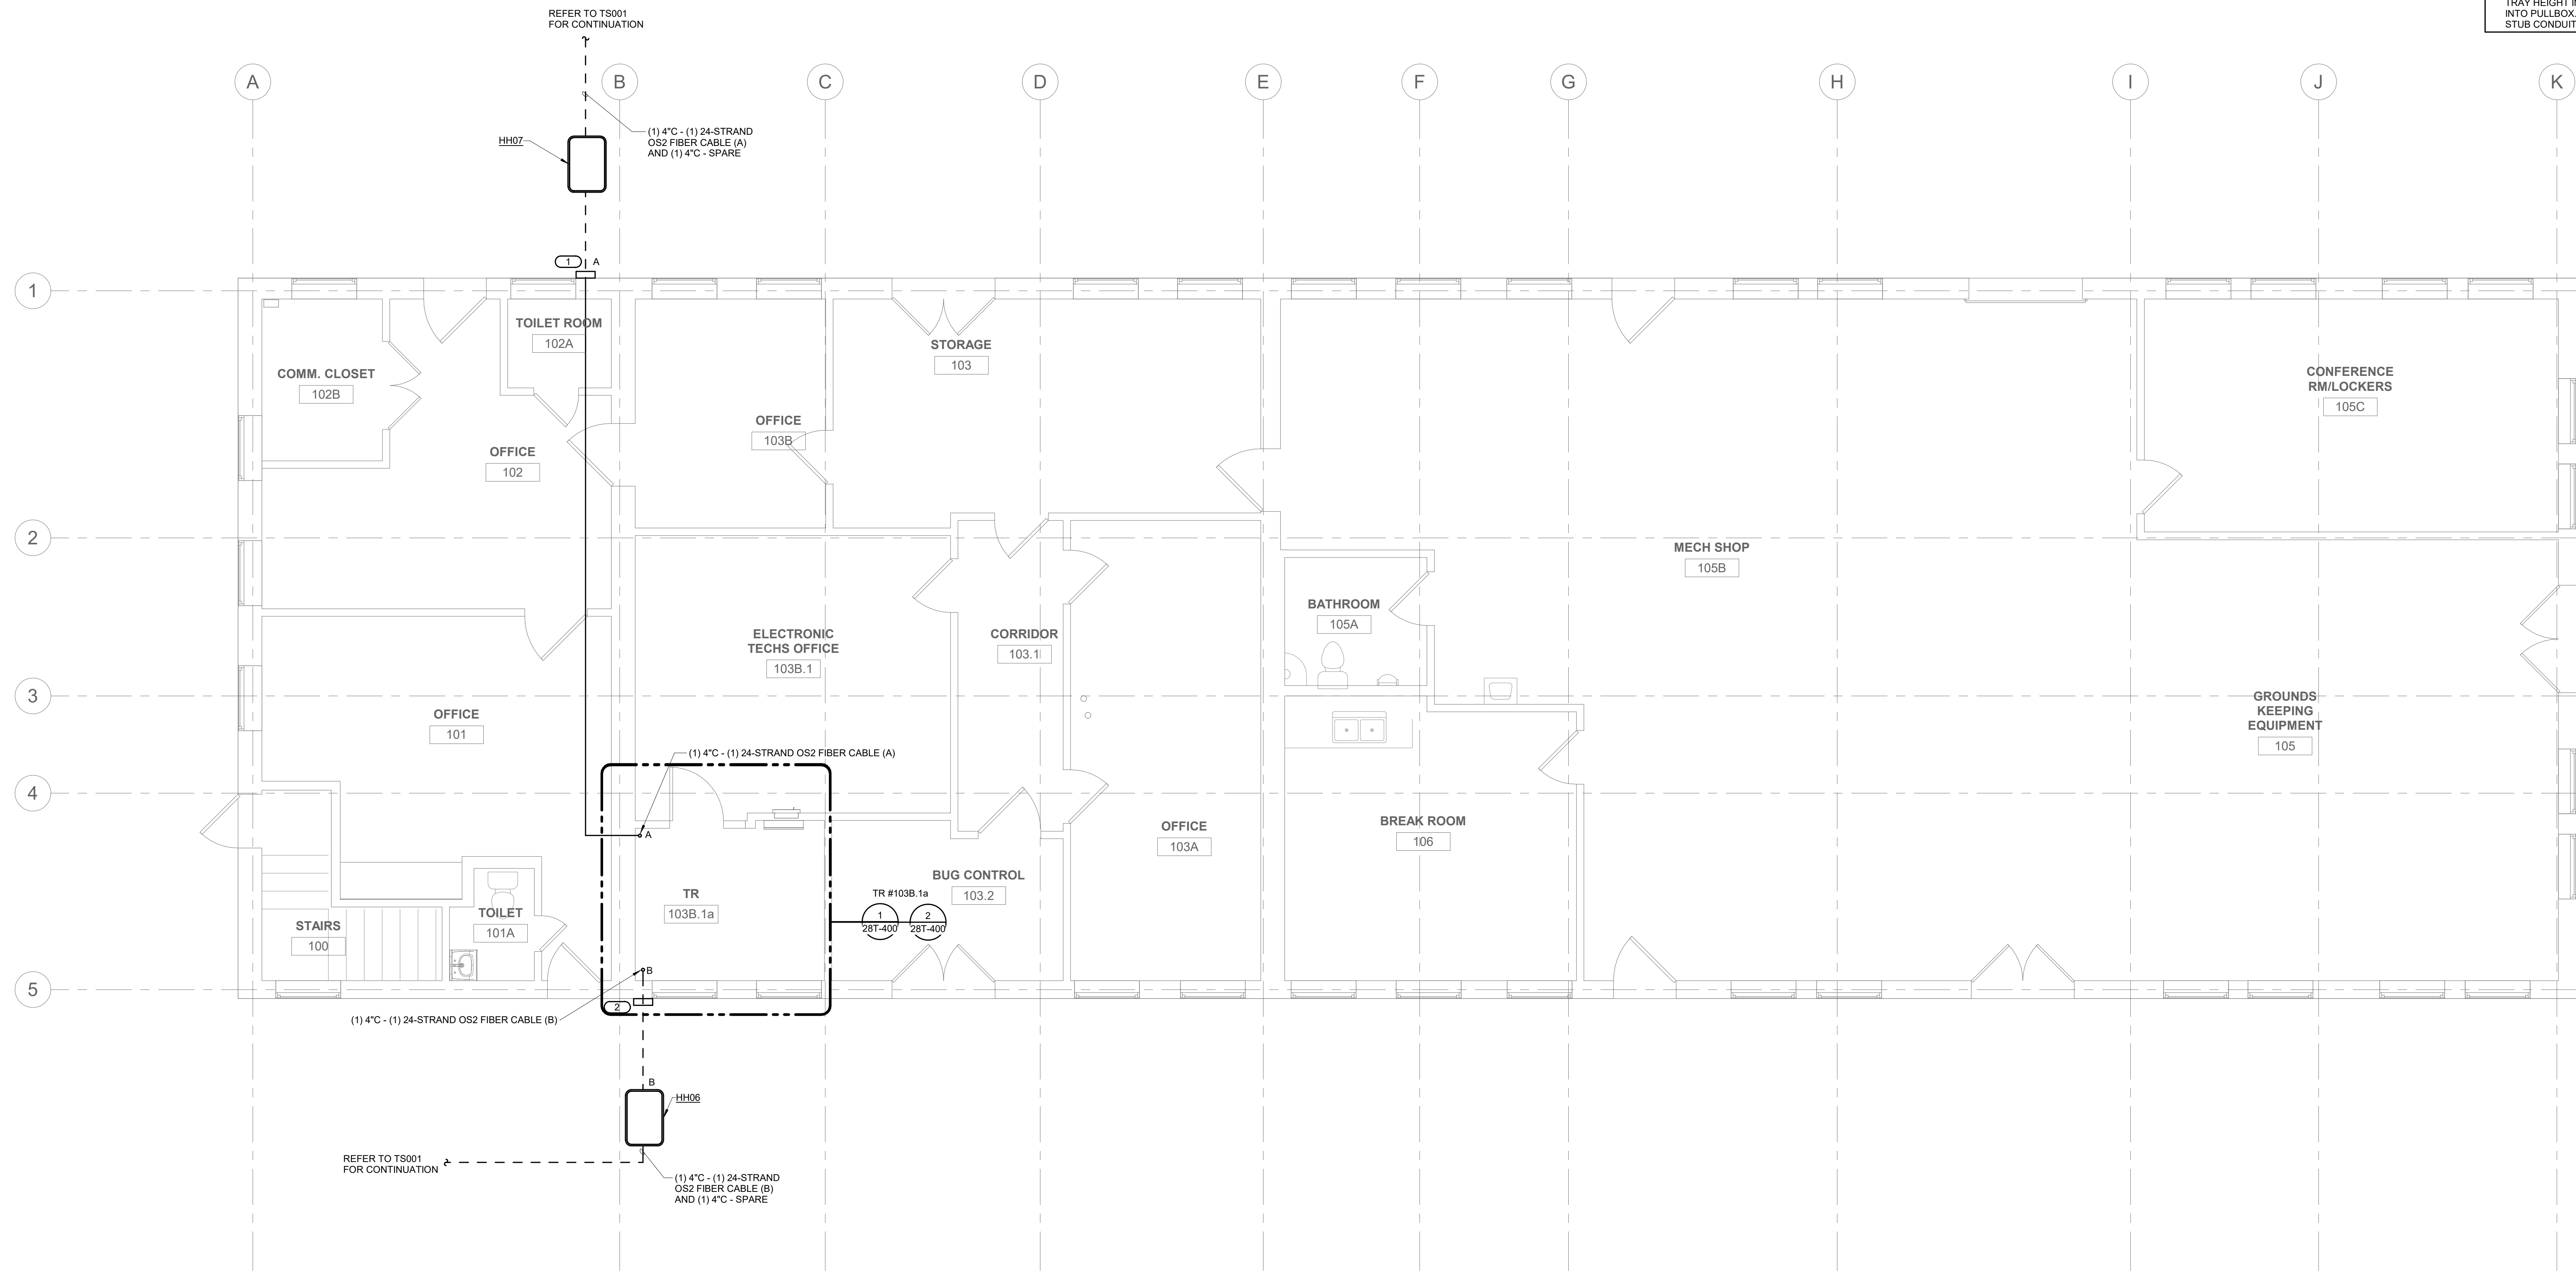

1 LEVEL 01 PLAN - TECHNOLOGY
1/4" = 1'-0"

--	--	

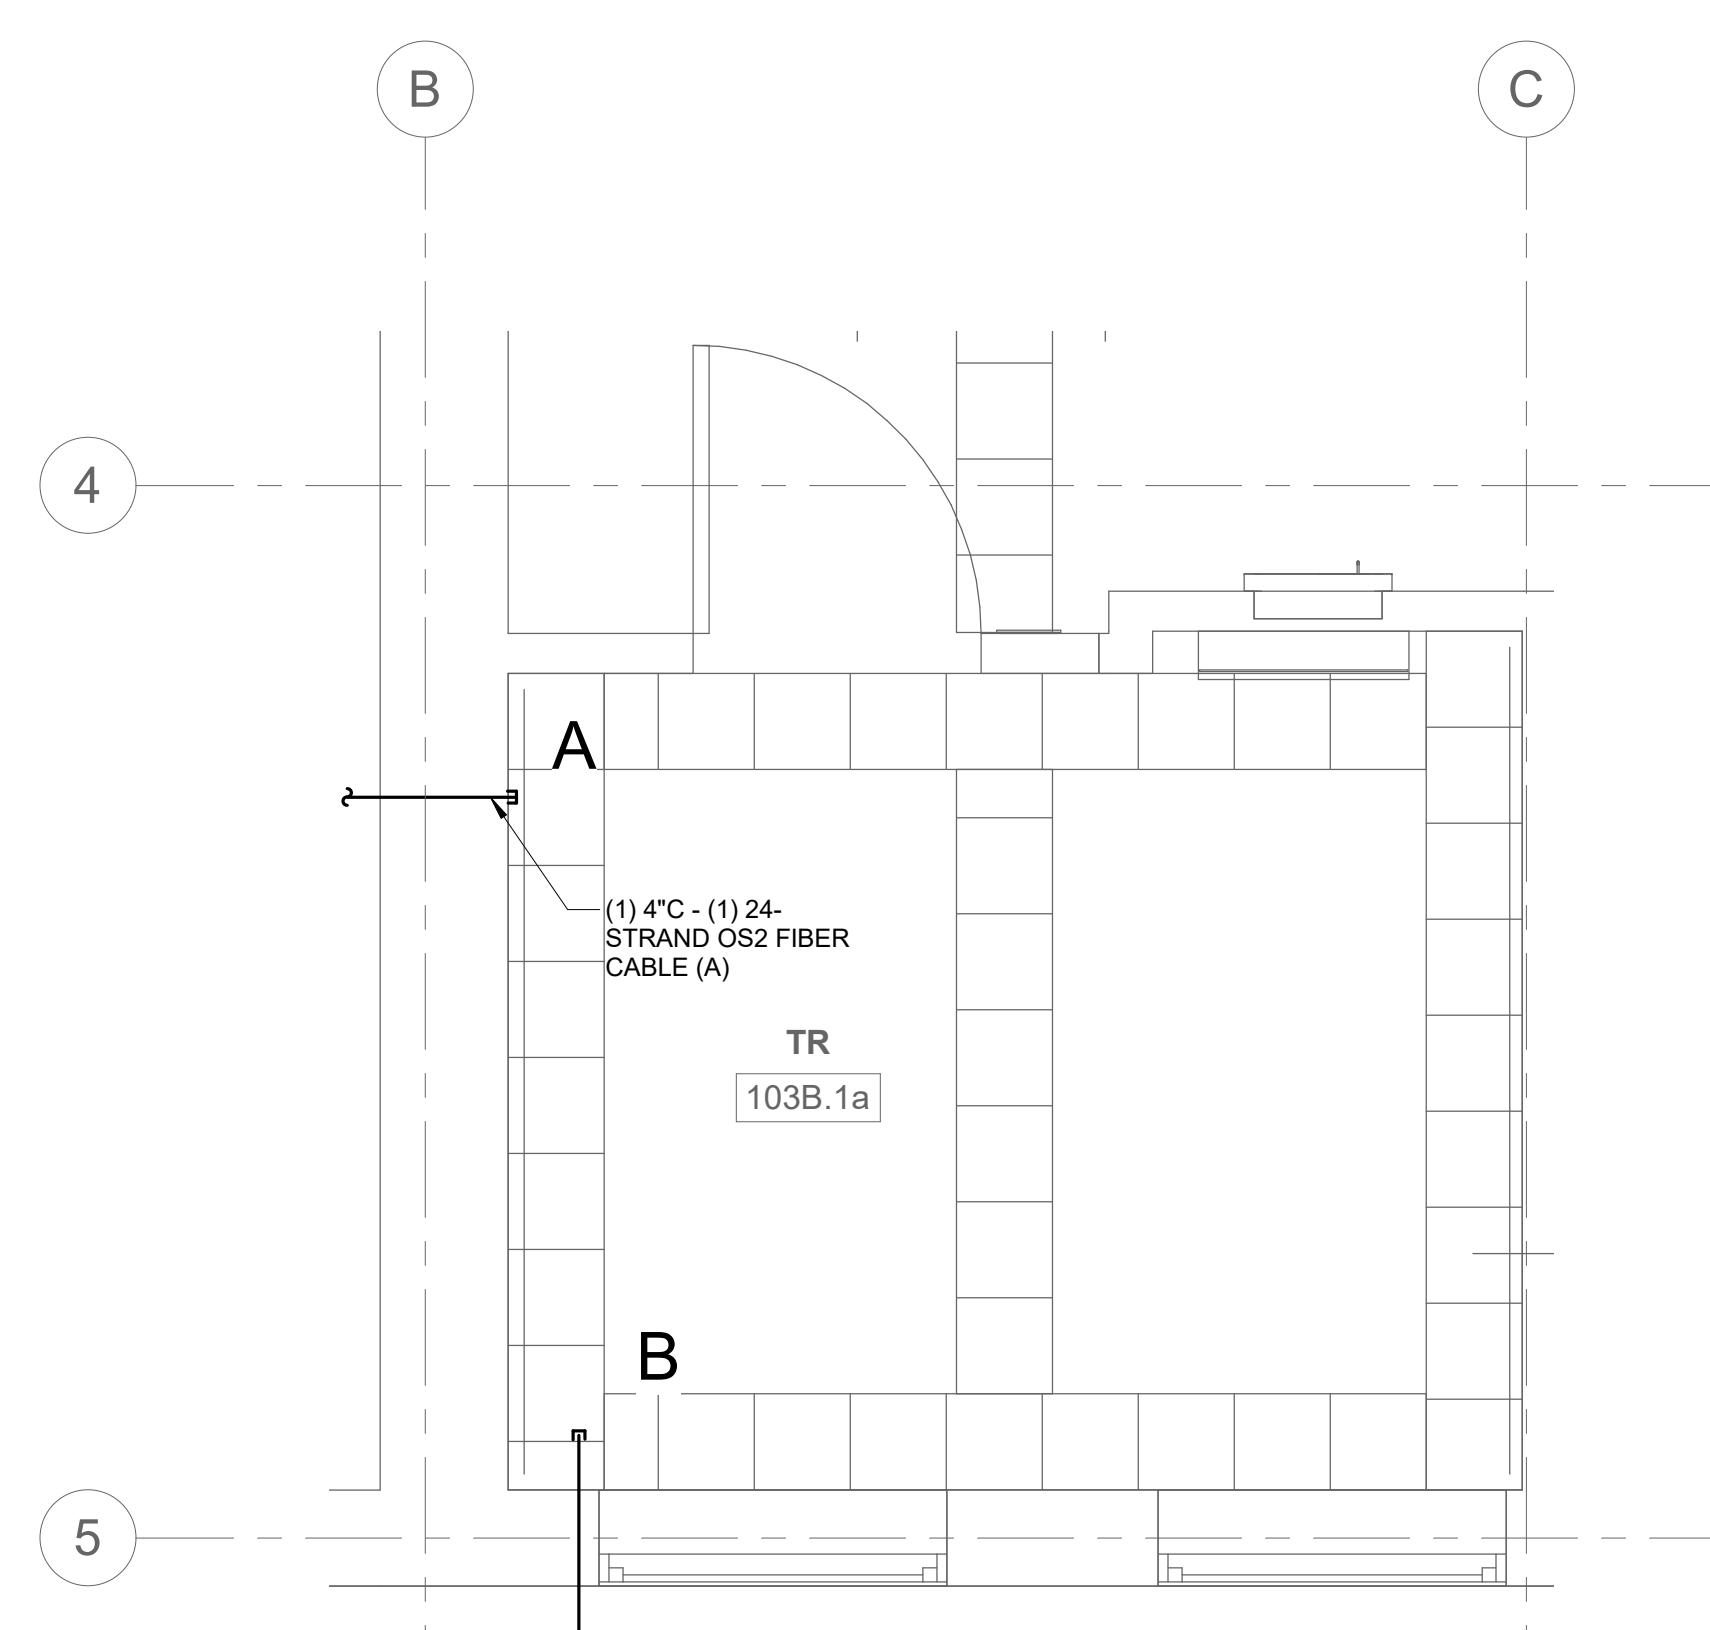

 **2** **TELECOM ROOM PATHWAY TR #103B.1a**
1/2" = 1'-0"

- KEY NOTES:** #
1. THROUGH WALL PENETRATION FOR BACKBONE CONDUIT. OPTICAL FIBER CABLE CONTINUES ON CABLE TRAY TO RACKS.



1. THIS RISER IS DIAGRAMMATIC AND MAY NOT SHOW ACTUAL ROUTING OR QUANTITIES OF ELECTRICAL WIRING. THIS RISER IS SHOWN FOR CLARIFICATION OF CONNECTION(S), LOCATIONS AND CABLE TYPE. ALL INFORMATION OUTLETS ARE TYPICAL OF THE OUTLETS IN THE AREA SHOWN. REFER TO FLOOR PLANS FOR MORE SPECIFIC ROUTING INFORMATION. REFER TO SPECIFICATIONS FOR ADDITIONAL REQUIREMENTS.
2. REFER TO ELECTRICAL DRAWINGS FOR CHANNEL RACK AND FIBER OPTIC DISTRIBUTION CABINET SPECIFICATIONS

[illegible]

- SHEET NOTES:
1. REFER TO TS001 FOR ADDITIONAL INFORMATION.

2. REFER TO TS00 AND TS01 FOR CAMPUS OPTICAL FIBER CABLE RISER DIAGRAMS.


3. REFER TO 271400 FOR HANDHOLE DETAIL.

4. NEW BACKBONE OPTICAL FIBER CABLES SHALL BE INDOOR/OUTDOOR TYPE.

5. ALL BACKBONE OPTICAL FIBER CABLE PATHWAYS SHALL BE NEW. DO NOT RE-USE EXISTING BACKBONE CABLE PATHWAYS FOR NEW BACKBONE CABLES.

6. TRANSITION PVC CONDUITS TO GRC IN CRAWL SPACE OR EXPOSED EXTERIOR LOCATIONS. TRANSITION TO EMT CONDUITS AT INTERIOR OF BUILDING. SEAL ALL PENETRATIONS TO MAINTAIN FIRE-RATINGS OF WALL, CEILING AND FLOORS.
- KEY NOTES: (#)
1. PROVIDE PULLBOX ON EXTERIOR WALL AT HEIGHT OF BASEMENT FLOOR CEILING. ROUTE CONDUITS UP ALONG WALL TO PULLBOX. PROVIDE PENETRATIONS THRU WALL. ROUTE CONDUITS THRU PULLBOX INTO BLDG 31.

2. CONTINUE ROUTE OF CONDUITS UP TO BASEMENT CEILING DECK. PROVIDE PENETRATION THRU CEILING AND ROUTE CONDUITS UP TO CEILING AND OVER TO LOCATION INDICATED BELOW FIRST FLOOR STORAGE ROOM. FIELD VERIFY EXACT LOCATION.

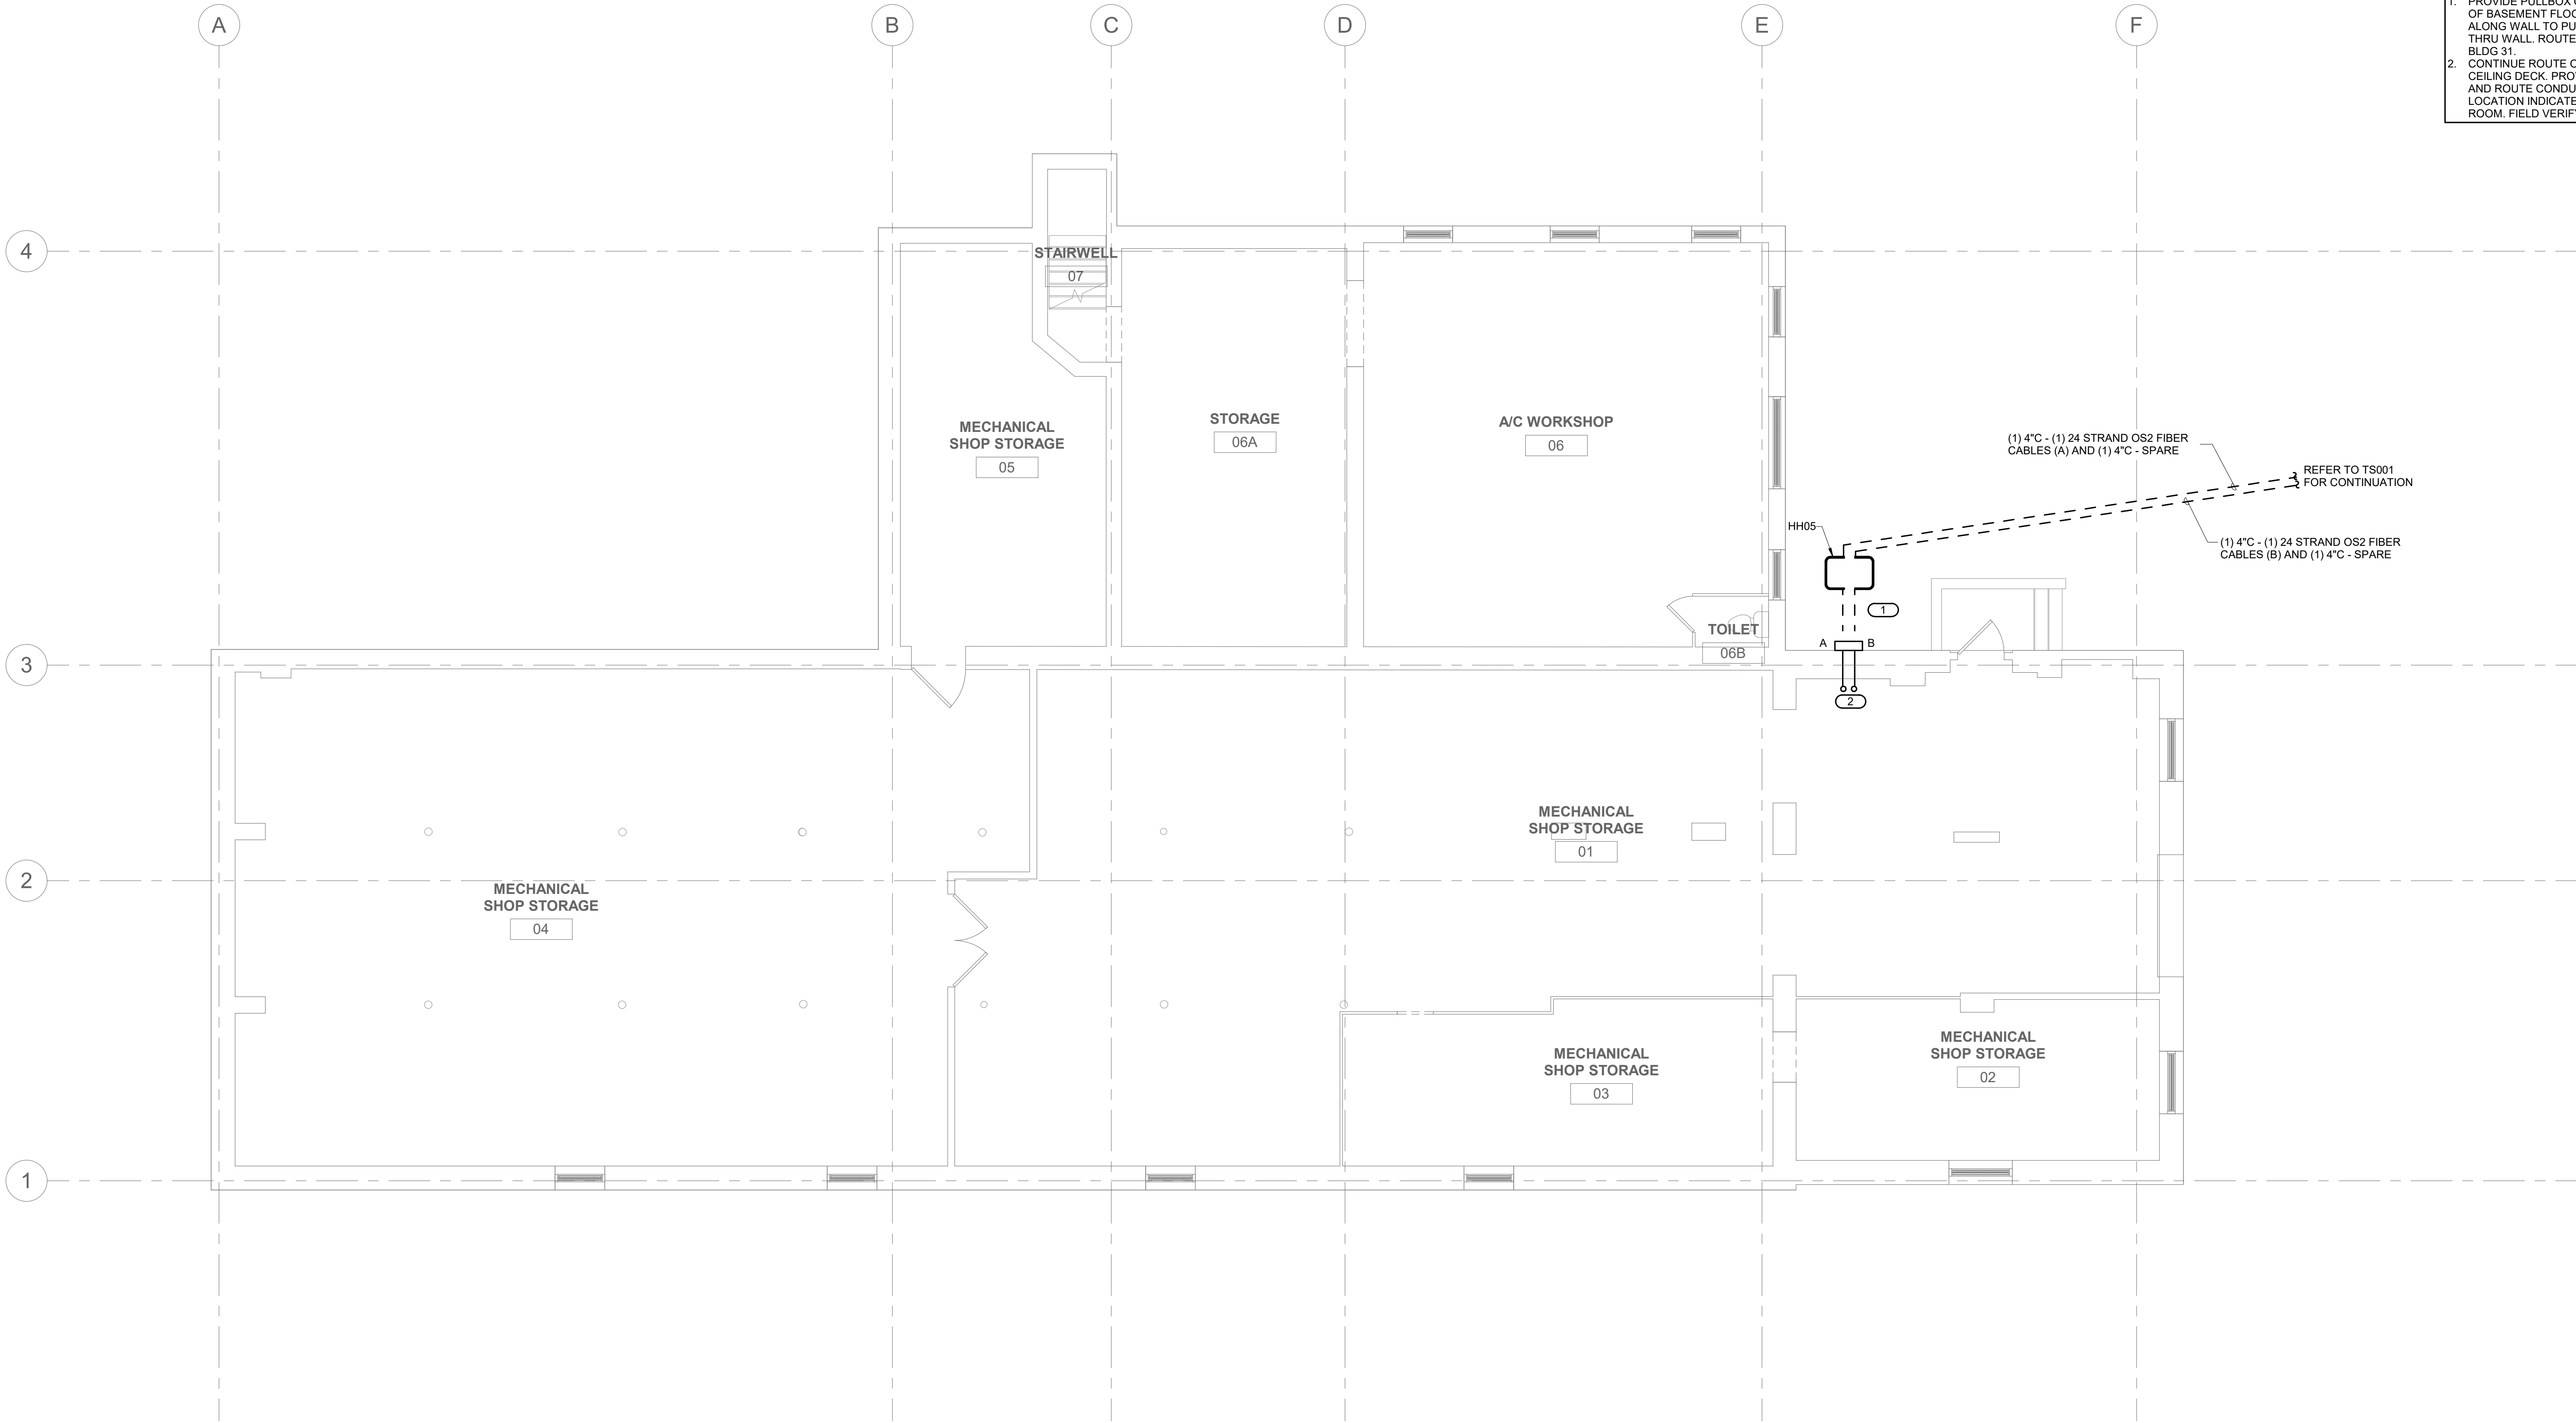

1

3/16" = 1'-0"

NORTH

BASMENT PLAN - TECHNOLOGY

Revisions: <table><tr><td> </td><td> </td></tr><tr><td> </td><td> </td></tr><tr><td> </td><td> </td></tr><tr><td> </td><td> </td></tr><tr><td> </td><td> </td></tr></table>											Date: <table><tr><td> </td></tr><tr><td> </td></tr><tr><td> </td></tr><tr><td> </td></tr><tr><td> </td></tr></table>						CONSULTANT ENGINEERING DISCIPLINE: IMEG www.imegcorp.com 225 W WASHINGTON STREET SUITE 2700 CHICAGO, IL 60606 P: 312.294.0501 F: 312.294.0003 PROJECT #22010109.00	ARCHITECT/ENGINEER OF RECORD A/E: SPEES DESIGN BUILD 23830 PACIFIC HIGHWAY S. SUITE 203 KENT, WA 98032 SDB SPEESDESIGNBUILD	STAMP REGISTERED COMMUNICATIONS DISTRIBUTION DESIGNER Bicsi ES-96-C WME-J Exp. No. 1519026 EXPIRES 03-01-2025 RCDD	Office of Construction and Facilities Management VA U.S. Department of Veterans Affairs	Drawing Title BLDG.31 BASEMENT PLAN - TECHNOLOGY Approved:	Phase 100% CONSTRUCTION DOCUMENTS FULLY SPRINKLERED	Project Title EHRM INFRASTRUCTURE UPGRADES - HAMPTON Location HAMPTON VA MEDICAL CENTER, HAMPTON, VIRGINIA Issue Date 05/09/2025 Checked EW Drawn IMEG	Project Number 509-22-700 Building Number 31 Drawing Number 31T-100 648 of 713

- SHEET NOTES:
1. REFER TO TS001 FOR ADDITIONAL INFORMATION.

2. REFER TO TS00 AND TS01 FOR CAMPUS OPTICAL FIBER CABLE RISER DIAGRAMS.


3. REFER TO 271400 FOR HANDHOLE DETAIL.

4. NEW BACKBONE OPTICAL FIBER CABLES SHALL BE INDOOR/OUTDOOR TYPE.

5. ALL BACKBONE OPTICAL FIBER CABLE PATHWAYS SHALL BE NEW. DO NOT RE-USE EXISTING BACKBONE CABLE PATHWAYS FOR NEW BACKBONE CABLES.

6. TRANSITION PVC CONDUITS TO GRC IN CRAWL SPACE OR EXPOSED EXTERIOR LOCATIONS. TRANSITION TO EMT CONDUITS AT INTERIOR OF BUILDING. SEAL ALL PENETRATIONS TO MAINTAIN FIRE-RATINGS OF WALL, CEILING AND FLOORS.
- KEYNOTES: (C #)
1. ROUTE CONDUITS UP THRU FLOOR TO ABOVE STORAGE ROOM FINISHED CEILING. CONTINUE ROUTE OF CONDUITS ABOVE CEILING OVER TO TR #106.

2. STUB CONDUITS INTO TR #106 ABOVE CABLE TRAY. CONTINUE ROUTE OF FIBER CABLES ALONG CABLE TRAY TO RACK.

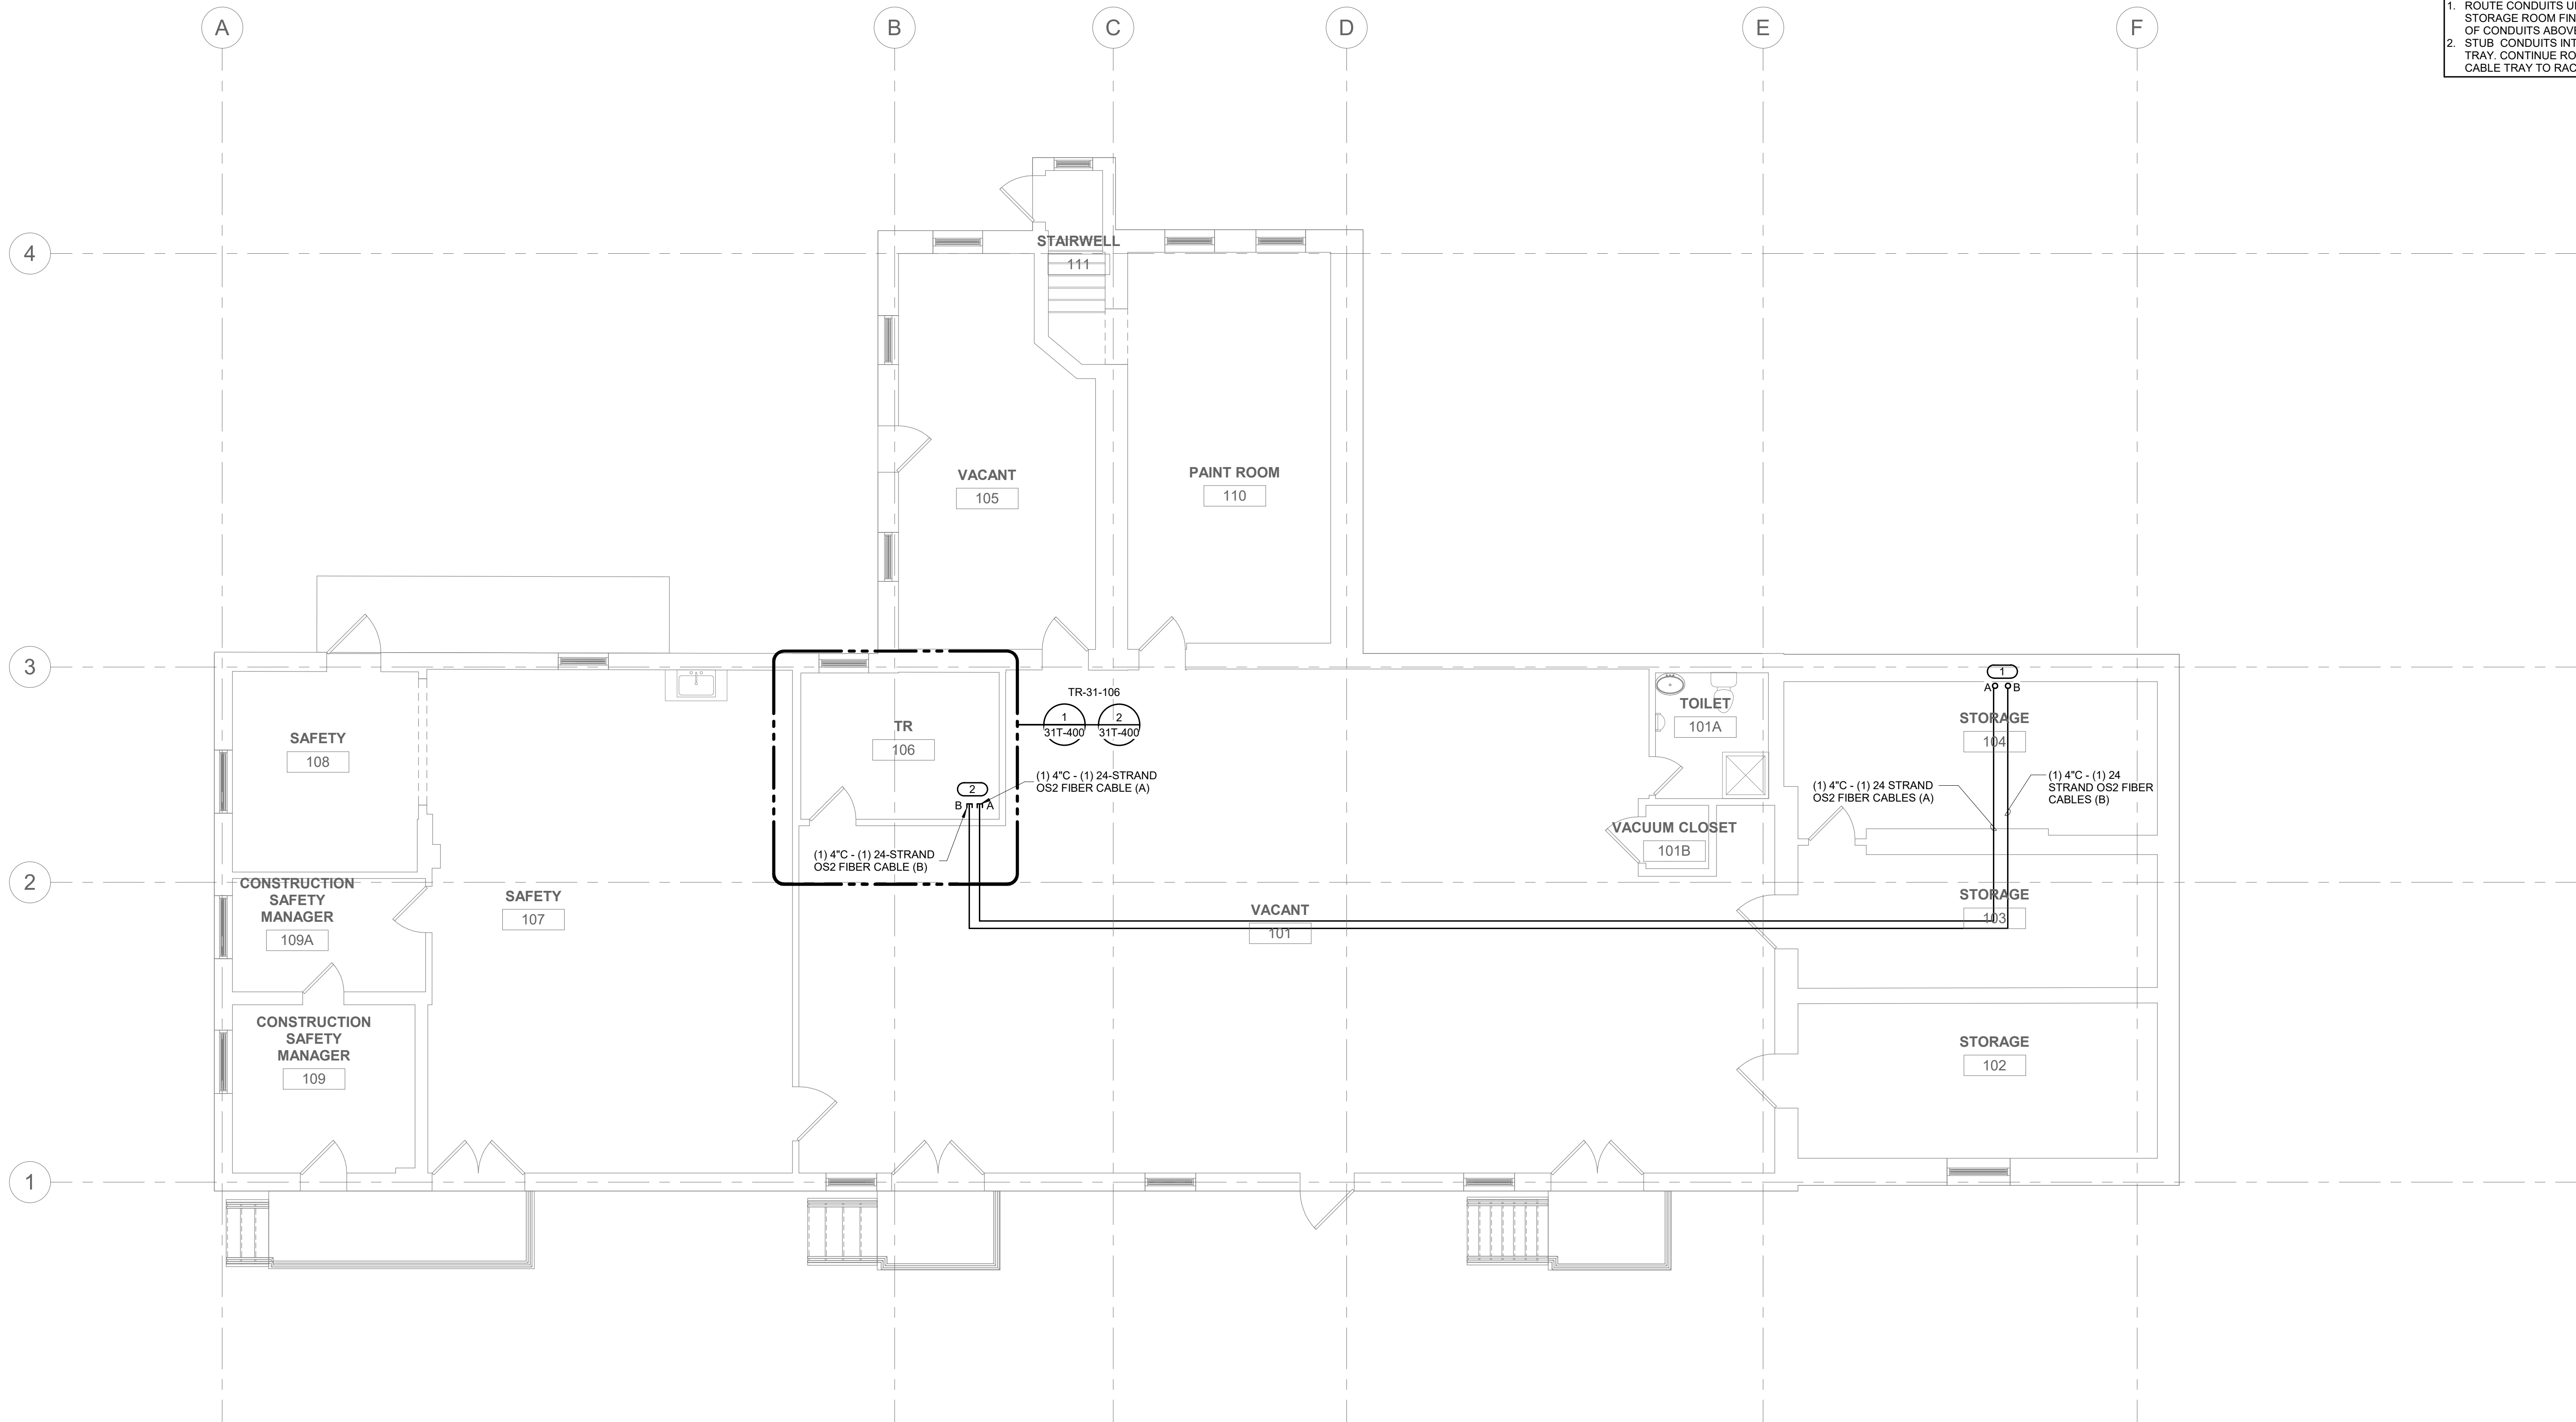

1 LEVEL 01 PLAN - TECHNOLOGY
3/16" = 1'-0"

		CONSULTANT	ARCHITECT/ENGINEER OF RECORD	STAMP	Office of Construction and Facilities Management	Drawing Title	Phase	Project Title	Project Number		
		ENGINEERING DISCIPLINE:	A/E:			BLDG.31 LEVEL 01 PLAN - TECHNOLOGY	100% CONSTRUCTION DOCUMENTS	EHRM INFRASTRUCTURE UPGRADES - HAMPTON	509-22-700		
						Approved:	FULLY SPRINKLERED	Location	Building Number		
		225 W WASHINGTON STREET SUITE 2700 CHICAGO, IL 60606 P: 312.294.0501 F: 312.294.0003 PROJECT #22010109.00	SPEEDSDSIGNBUILD				FULLY SPRINKLERED	HAMPTON VA MEDICAL CENTER, HAMPTON, VIRGINIA	31		
Revisions:	Date:				VA U.S. Department of Veterans Affairs			Issue Date	Checked	Drawn	Drawing Number
								05/09/2025	EW	IMEG	31T-101
											649 of 713

BLM 360/1509-22-700
VA Hampton
E:\M\509-22-700\B31.T_R21.rvt
8/21/2025 7:28:09 AM

VA FORM 08 - 6231

CONSULTANT

ENGINEERING DISCIPLINE:


www.imegcorp.com
225 W WASHINGTON STREET
SUITE 2700
CHICAGO, IL 60606
P: 312.294.0501 F: 312.294.0003
PROJECT #22010109.00

ARCHITECT/ENGINEER OF RECORD

A/E:

SPEES DESIGN BUILD
23830 PACIFIC HIGHWAY S. SUITE 203
KENT, WA 98032

 SPEESDESIGNBUILD

STAMP



Office of
Construction
and Facilities
Management

 U.S. Department
of Veterans Affairs

Drawing Title

BLDG.31 TECHNOLOGY DETAILS AND
DIAGRAMS

Approved:

Phase

100% CONSTRUCTION
DOCUMENTS

FULLY SPRINKLERED

Project Title

EHRM INFRASTRUCTURE
UPGRADES - HAMPTON

Location

HAMPTON VA MEDICAL CENTER, HAMPTON, VIRGINIA

Issue Date

05/09/2025

Checked

EW

Drawn

IMEG

Project Number

509-22-700

Building Number

31

Drawing Number

31T-400


650 of 713

SHEET NOTES:

1. REFER TO SITEPLAN TS001 FOR ADDITIONAL INFORMATION.
2. REFER TO T500 AND T501 FOR CAMPUS OPTICAL FIBER CABLE RISER DIAGRAMS.
3. REFER TO 2T400 FOR HANDHOLE DETAIL.
4. NEW BACKBONE OPTICAL FIBER CABLES SHALL BE INDOOR/OUTDOOR TYPE.
5. ALL BACKBONE OPTICAL FIBER CABLE PATHWAYS SHALL BE NEW. DO NOT REUSE EXISTING BACKBONE CABLE PATHWAYS FOR NEW BACKBONE CABLES.
6. TRANSITION PVC CONDUITS TO GRC IN CRAWL SPACE OR EXPOSED EXTERIOR LOCATIONS. TRANSITION TO EMT CONDUIT AT INTERIOR OF BUILDING. SEAL ALL PENETRATIONS TO MAINTAIN FIRE-RATINGS OF WALL, CEILING AND FLOORS.

KEY NOTES: #

1. PROVIDE PULLBOX ON EXTERIOR WALL AT HEIGHT ABOVE FINISHED CEILING. ROUTE CONDUIT UP WALL INTO PULLBOX. PROVIDE PENETRATION THRU WALL AND ROUTE CONDUIT THRU WALL ABOVE CEILING INTO TR # 105.
2. PROVIDE PULLBOX ON EXTERIOR WALL ABOVE CABLE TRAY HEIGHT IN TR #105 ROUTE CONDUIT UP WALL INTO PULLBOX. PROVIDE PENETRATION THRU WALL AND STUB CONDUIT ABOVE CABLE TRAY.
3. TR #105 SHALL SERVE NETWORK DEVICES ON FLOOR ABOVE.

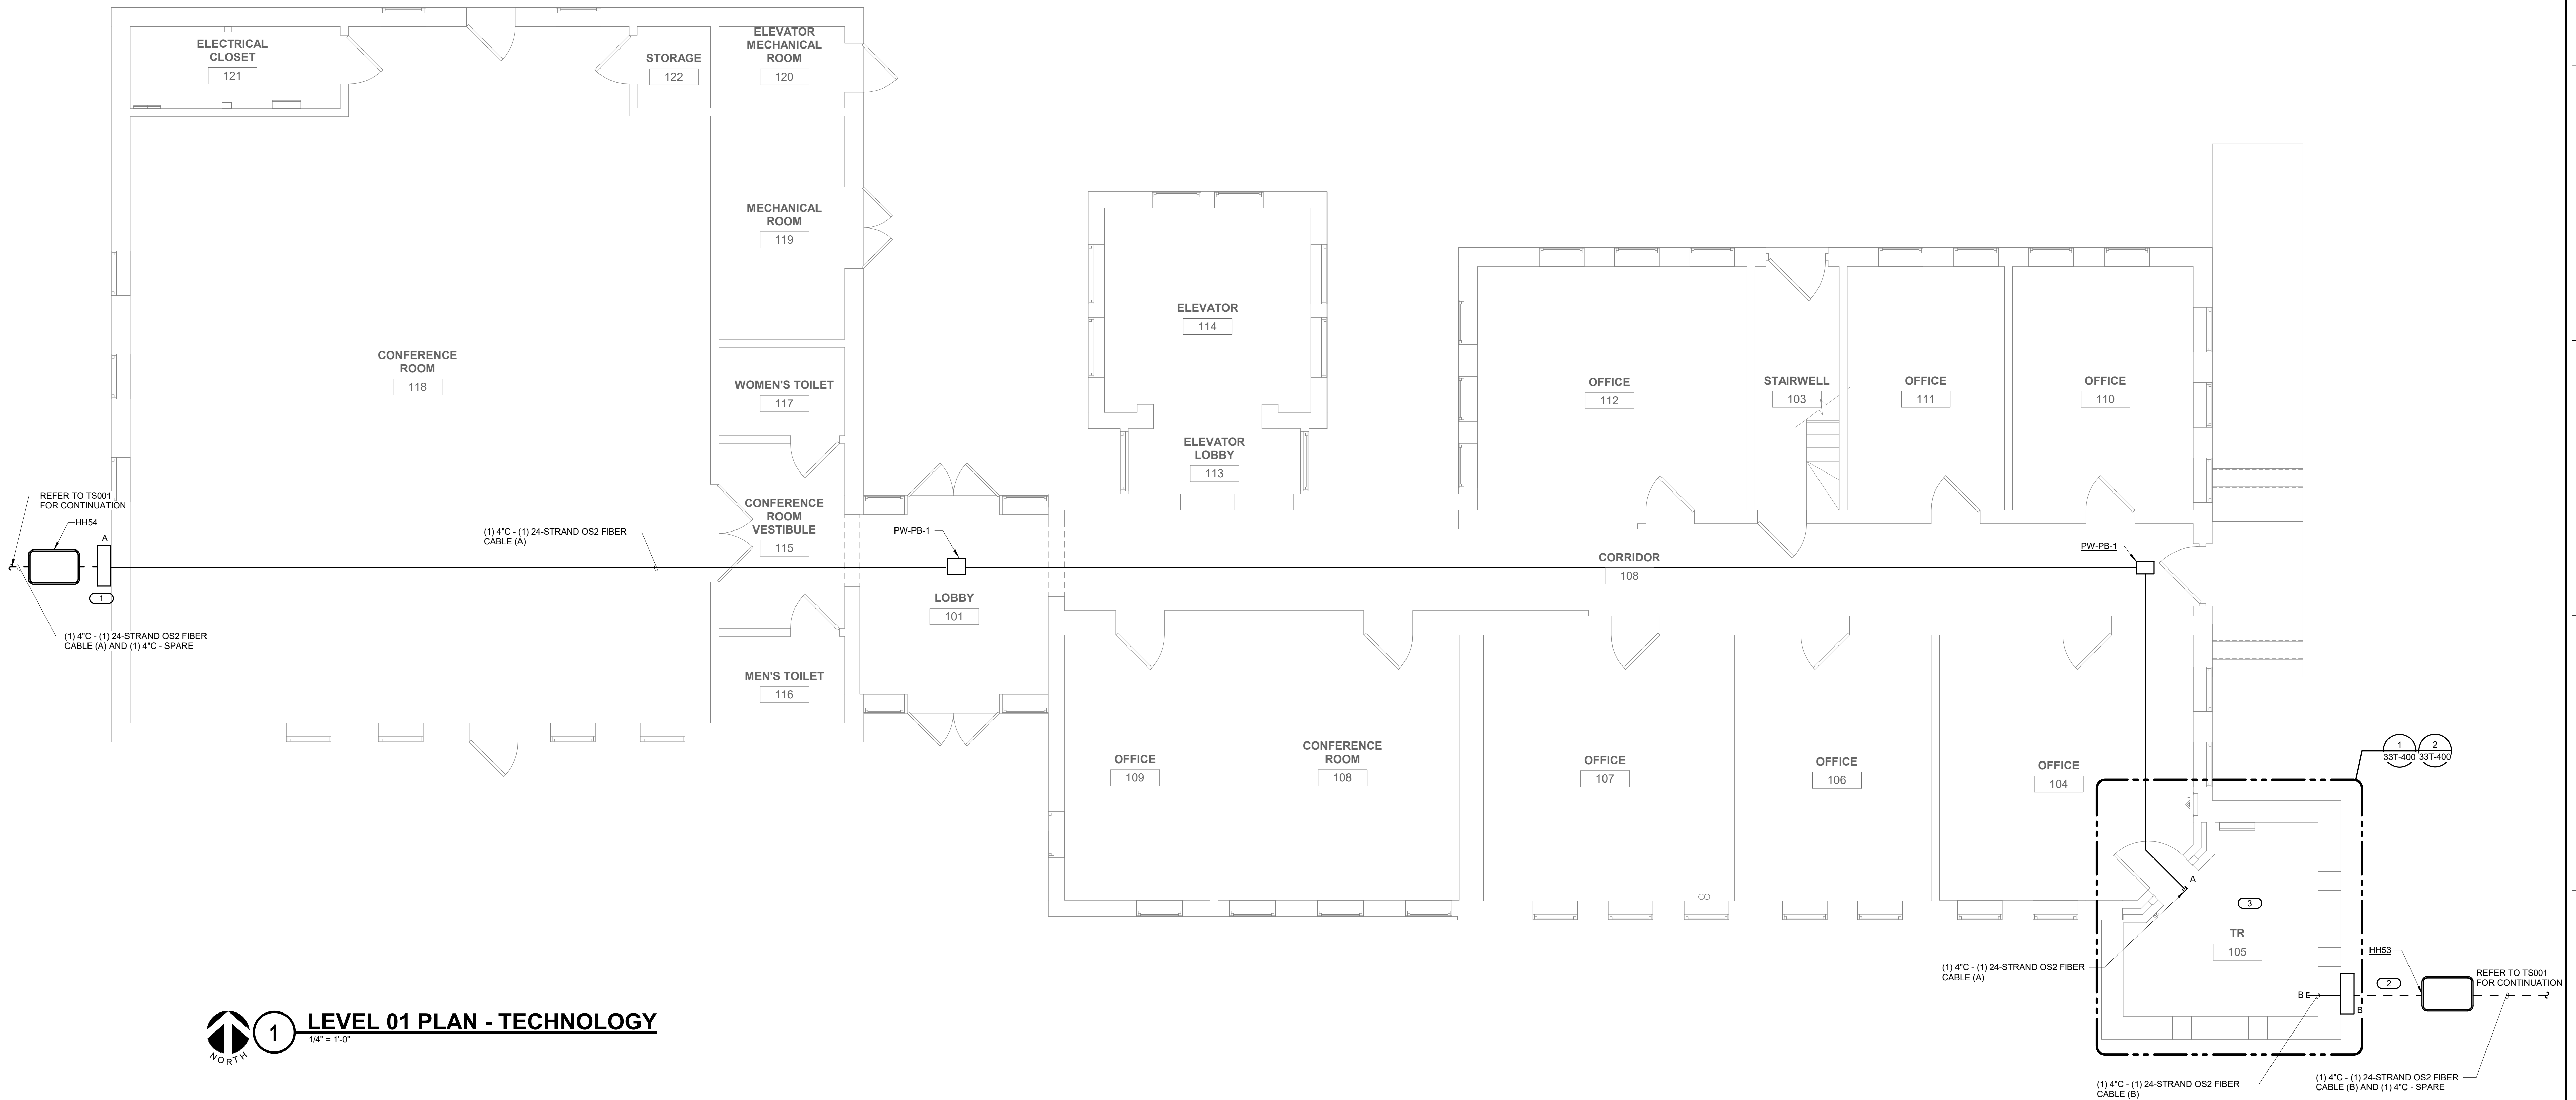

1

LEVEL 01 PLAN - TECHNOLOGY

$$1/4'' = 1'-0''$$
[illegible]

A

B

C

D

E

F


A

B

C

D

E

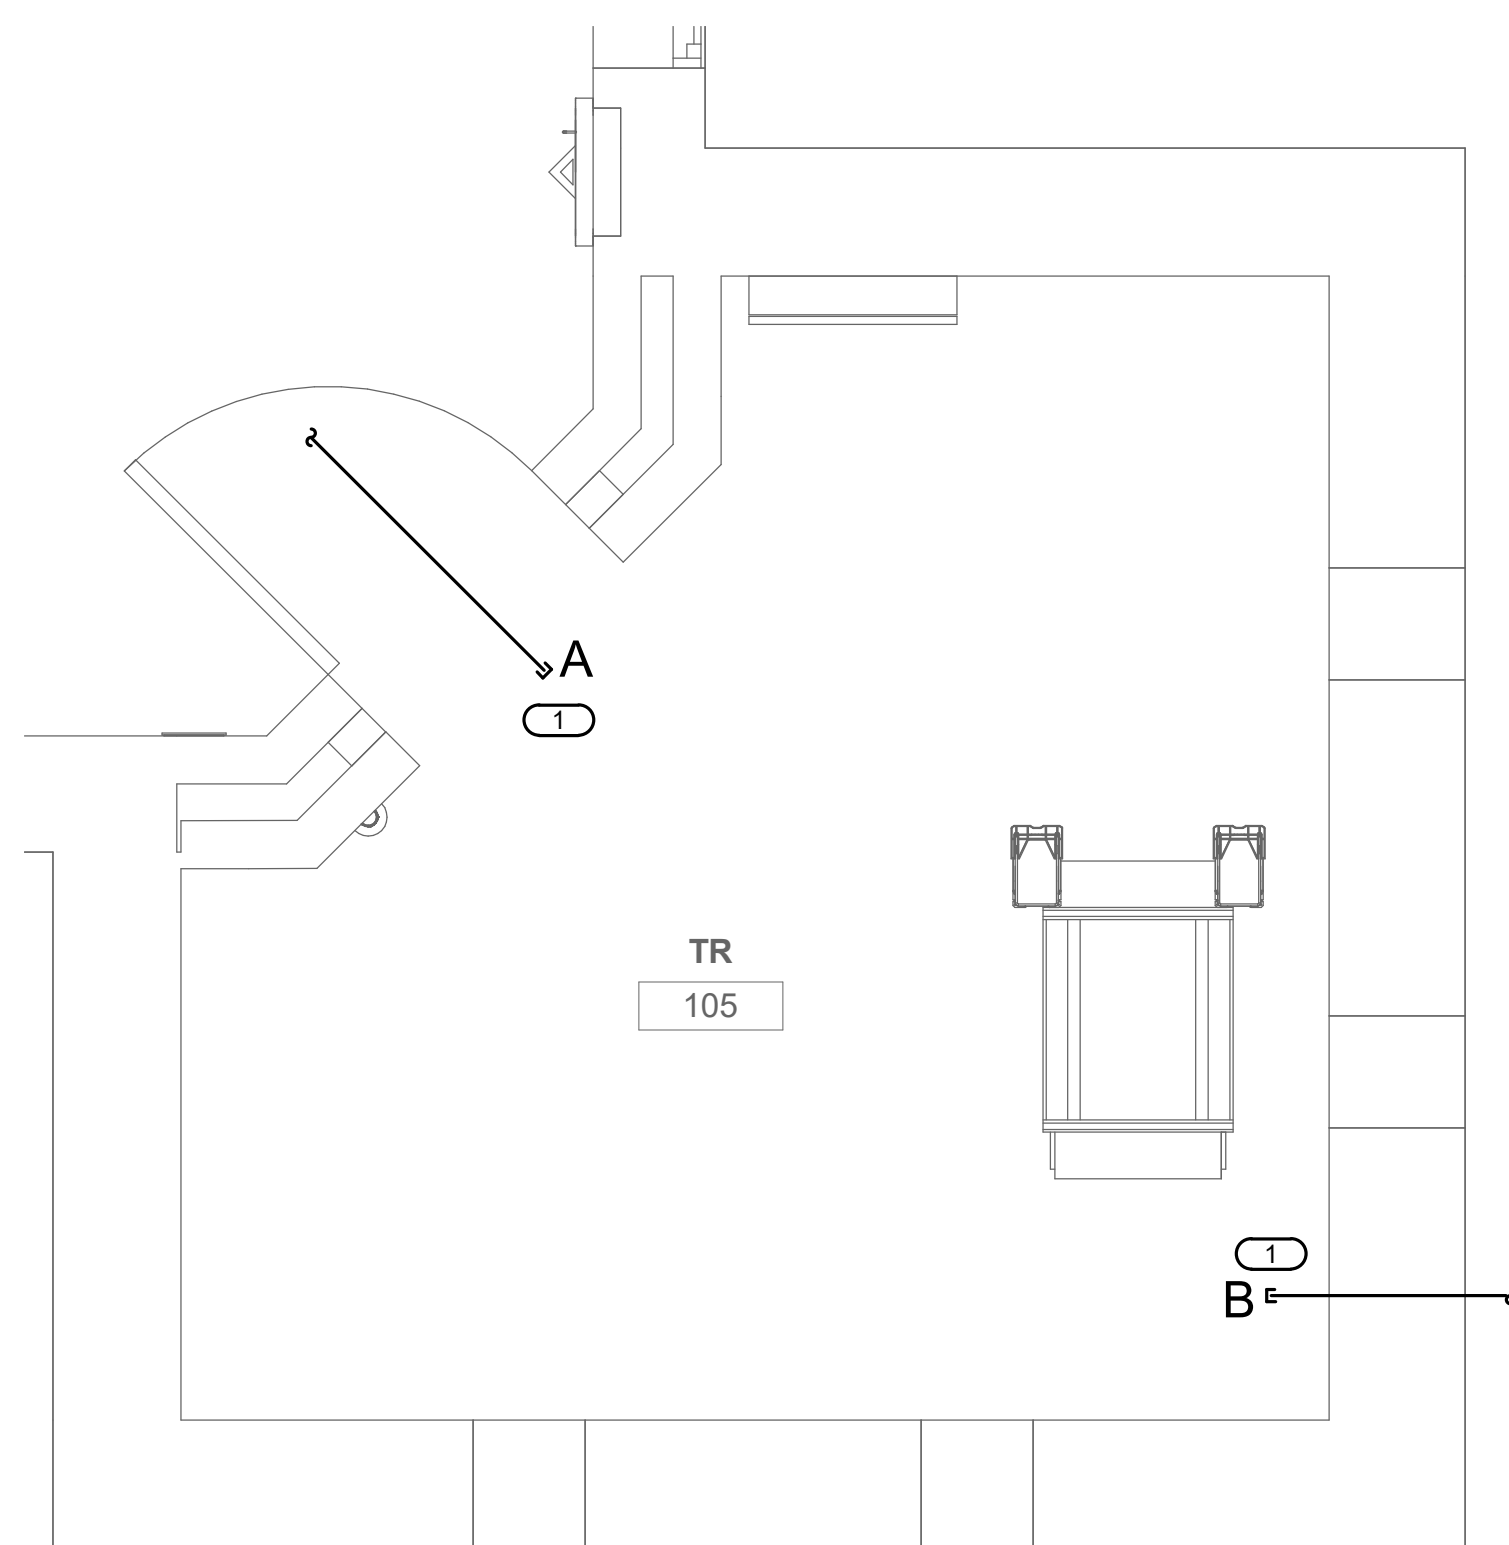F

1

TELECOM ROOM ENLARGEMENT TR #105


$1/2'' = 1'-0''$

NOTES:

1. REFER TO ELECTRICAL DRAWINGS FOR ROOM LAYOUT AND RACK ELEVATIONS.
2. ROUTE OPTICAL FIBER CABLE TO OVERHEAD CABLE TRAY AND TERMINATE IN FIBER DISTRIBUTION CABINET.

KEY NOTES: #


1. THROUGH WALL PENETRATION FOR BACKBONE CONDUIT. OPTICAL FIBER CABLE CONTINUES ON CABLE TRAY TO RACKS.

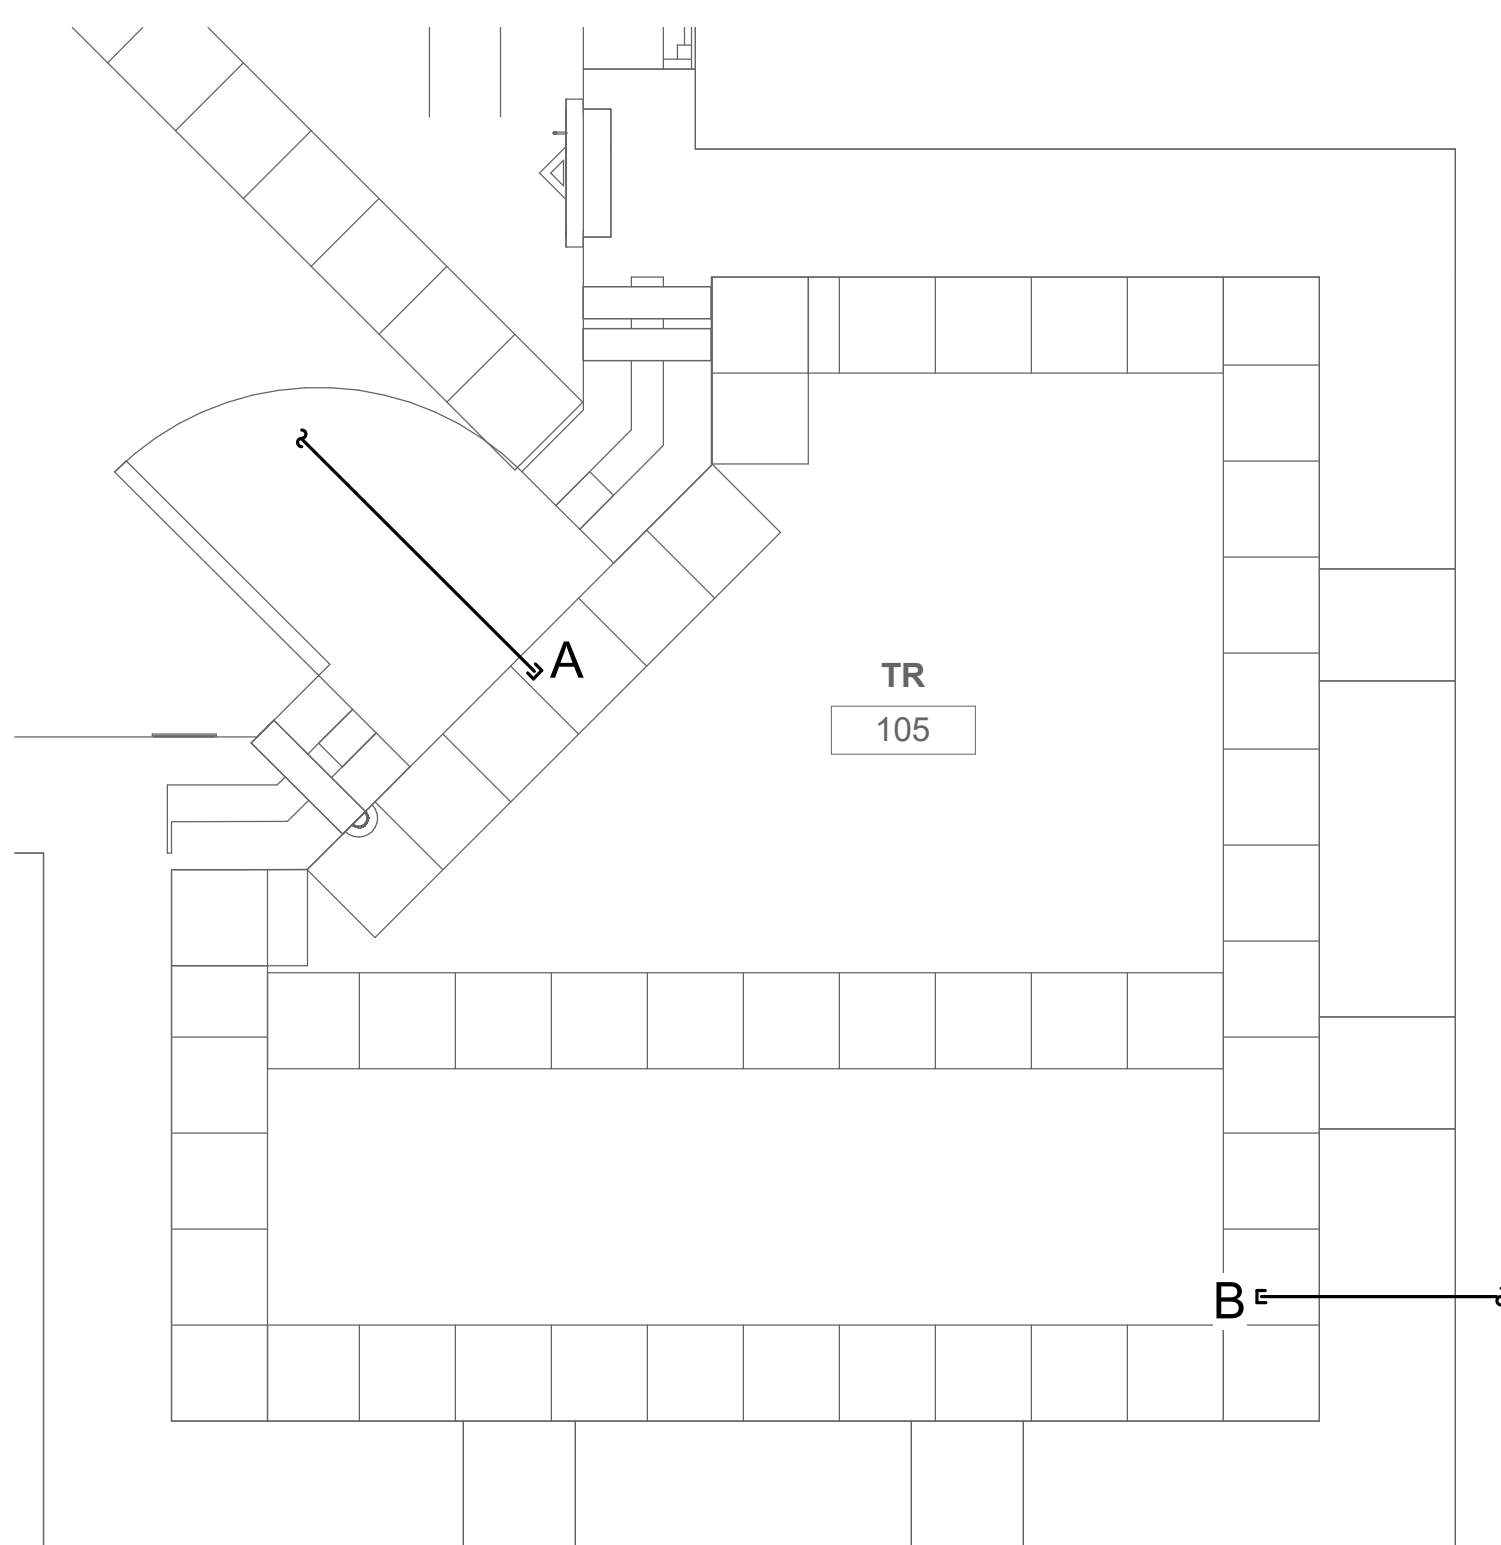


2

TELECOM ROOM PATHWAY TR #105

1/2" = 1'-0"

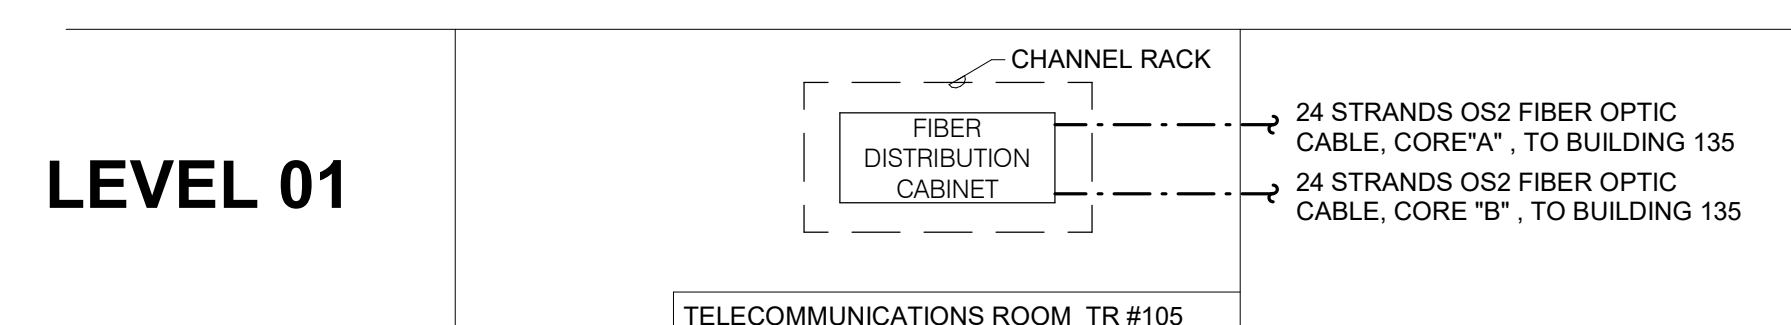

LEVEL 01

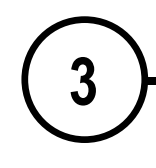

FIBER RISER DIAGRAM

NO SCALE

NOTES:

1. THIS RISER IS DIAGRAMMATIC AND MAY NOT SHOW ACTUAL ROUTING OR QUANTITIES OF MATERIALS SHOWN. THIS RISER IS SHOWN FOR CLARIFICATION OF CONNECTION(S), LOCATIONS AND CABLE TYPE. ALL INFORMATION OUTLETS ARE TYPICAL OF THE OUTLETS IN THE AREA SHOWN. REFER TO FLOOR PLANS FOR MORE SPECIFIC ROUTING INFORMATION. REFER TO SPECIFICATIONS FOR ADDITIONAL REQUIREMENTS.
2. REFER TO ELECTRICAL DRAWINGS FOR CHANNEL RACK AND FIBER OPTIC DISTRIBUTION CABINET SPECIFICATIONS

[illegible]

A
B
C
D
E
F

A
B
C
D
E
F

- SHEET NOTES:
1. REFER TO SITE PLAN TS001 FOR ADDITIONAL INFORMATION.

2. REFER TO T500 AND T501 FOR CAMPUS OPTICAL FIBER CABLE RISER DIAGRAMS.


3. REFER TO 277400 FOR HANDHOLE DETAIL.

4. NEW BACKBONE OPTICAL FIBER CABLES SHALL BE INDOOR/OUTDOOR TYPE.

5. ALL BACKBONE OPTICAL FIBER CABLE PATHWAYS SHALL BE NEW. DO NOT RE-USE EXISTING BACKBONE CABLE PATHWAYS FOR NEW BACKBONE CABLES.

6. TRANSITION PVC CONDUITS TO GRC IN CRAWL SPACE OR EXPOSED EXTERIOR LOCATIONS. TRANSITION TO EMT CONDUITS AT INTERIOR OF BUILDING. SEAL ALL PENETRATIONS TO MAINTAIN FIRE-RATINGS OF WALL, CEILING AND FLOORS.
- KEY NOTES: C #
1. PROVIDE PULL BOX ON EXTERIOR WALL AT HEIGHT ABOVE FINISHED CEILING. ROUTE CONDUIT UP WALL INTO PULLBOX. PROVIDE PENETRATION THRU WALL AND ROUTE CONDUIT THRU WALL ABOVE CEILING INTO TR # 1C.

2. TR #1C SHALL SERVE NETWORK DEVICES ON FLOOR ABOVE.

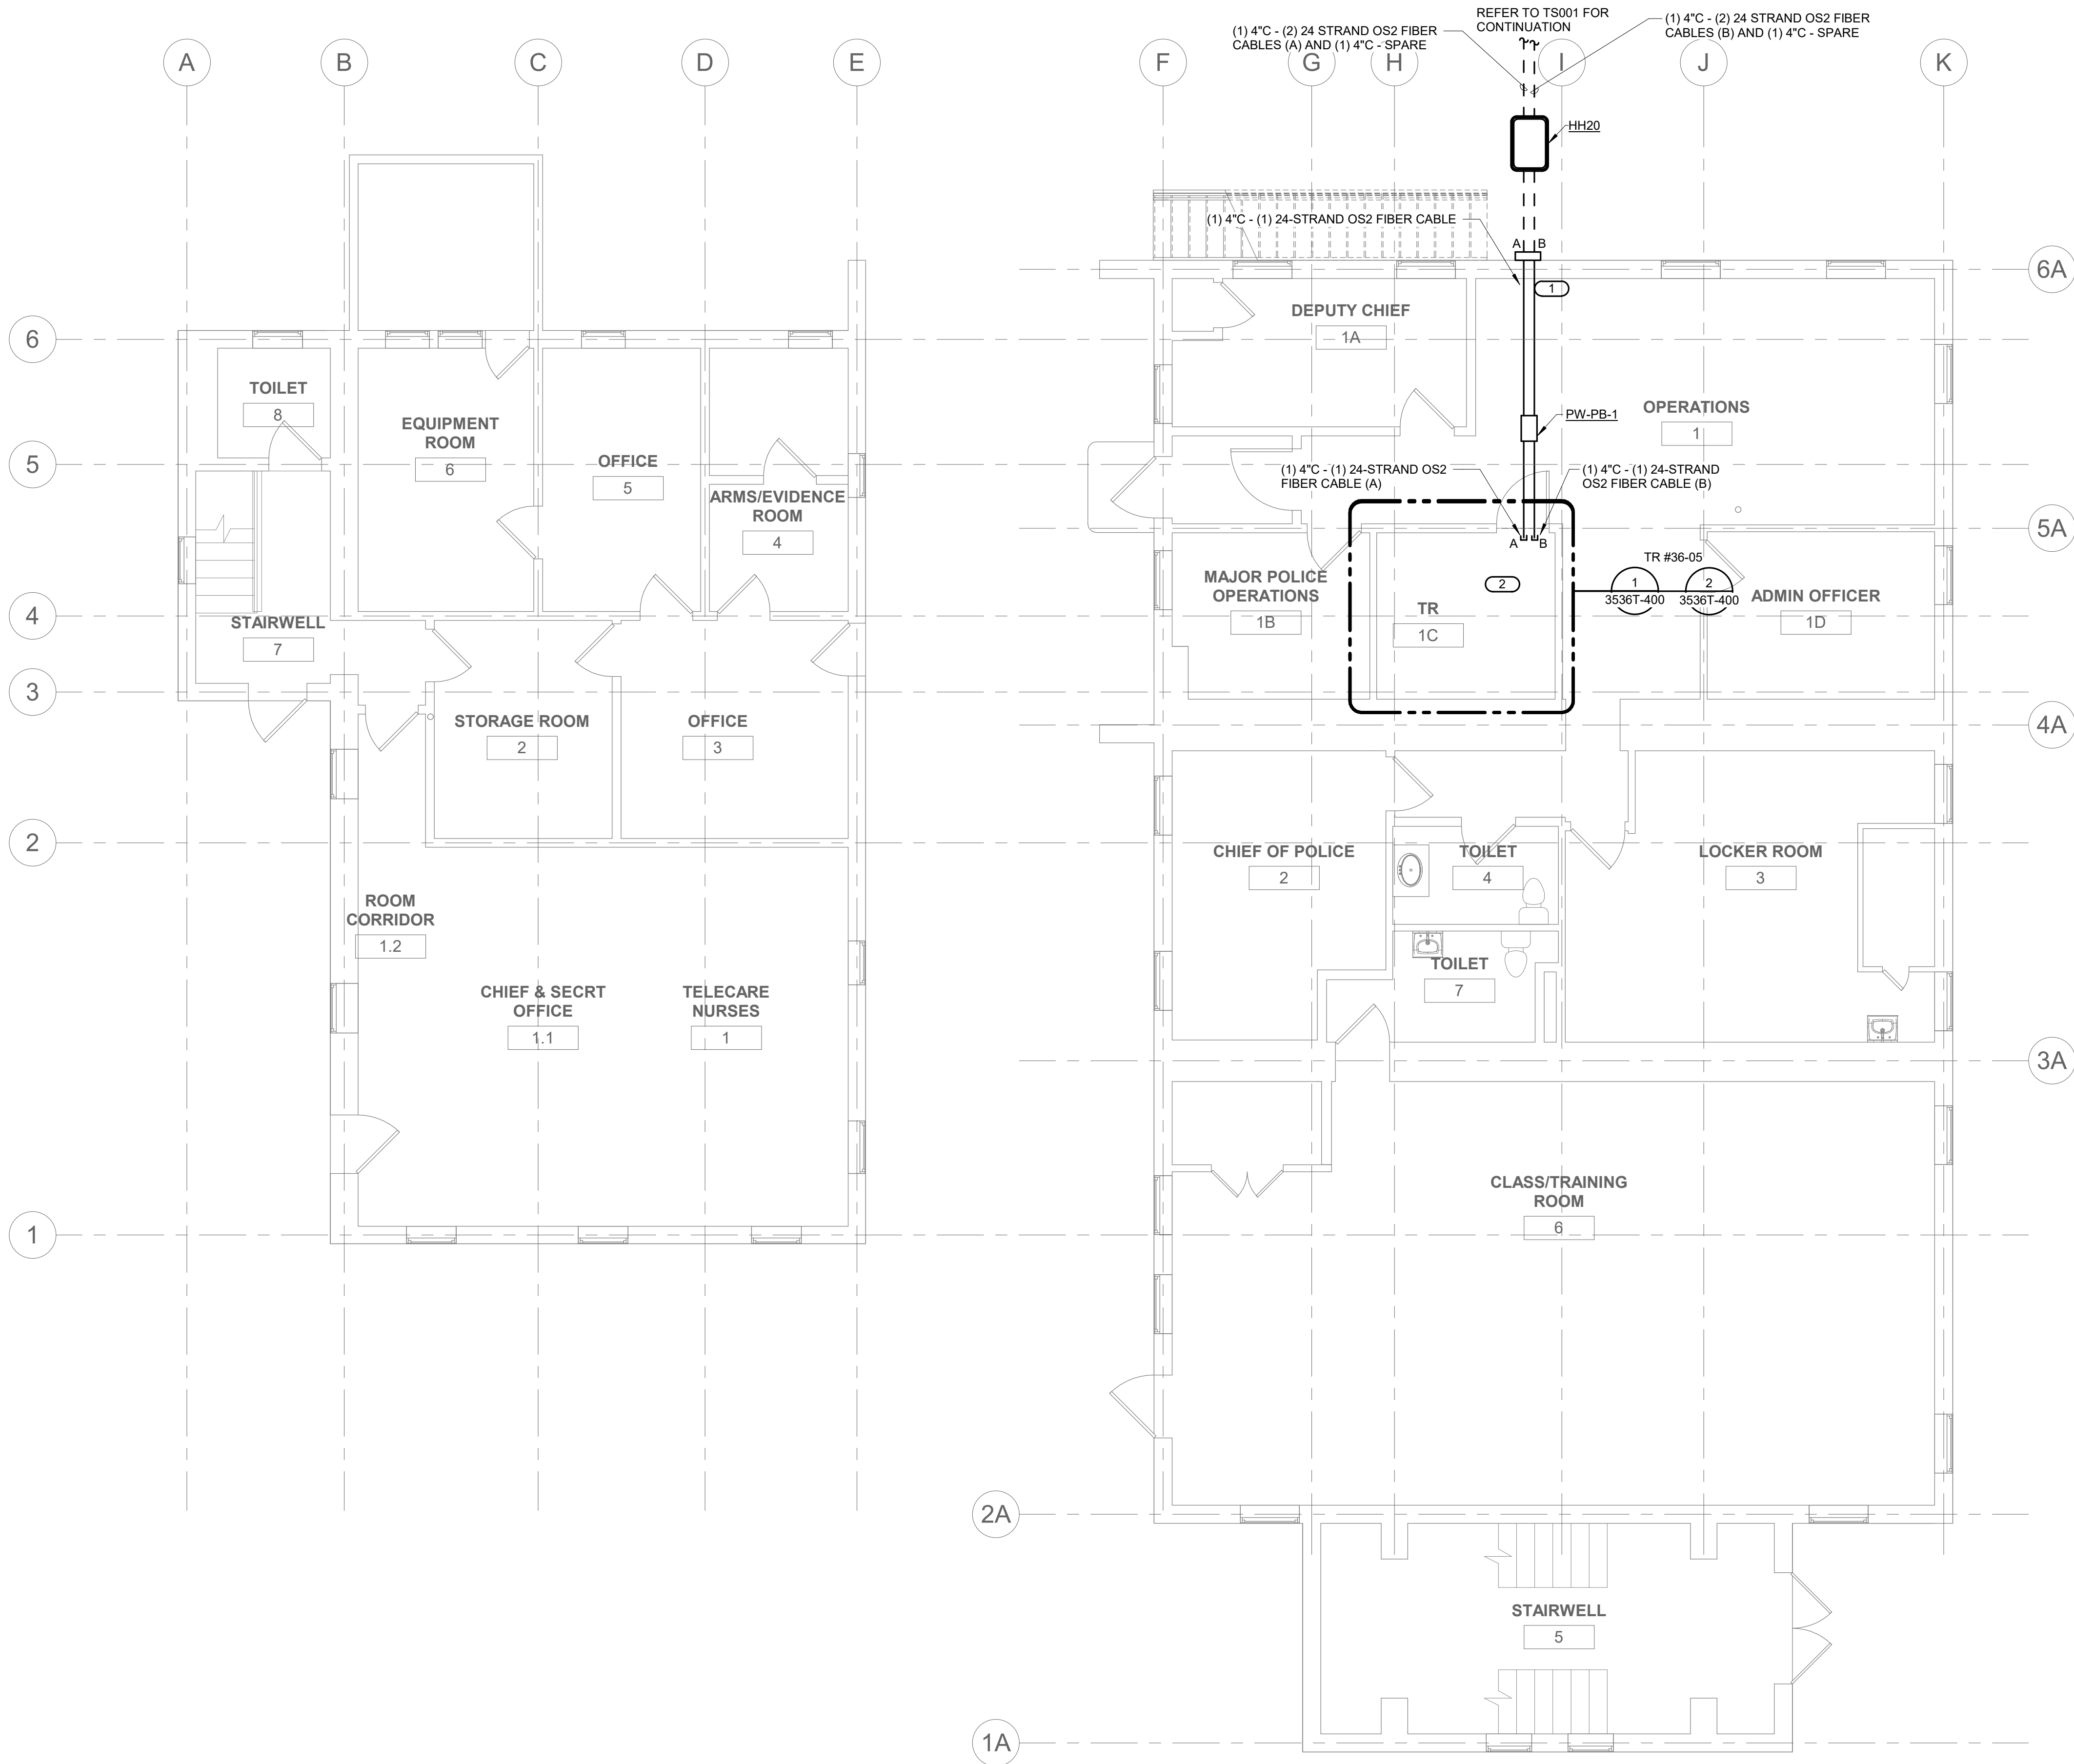

1

LEVEL 01 PLAN - TECHNOLOGY

3/16\" = 1'-0"

Revisions:	
Date:	

CONSULTANT
ENGINEERING DISCIPLINE:
IMEG
www.imegcorp.com
225 W WASHINGTON STREET
SUITE 2700
CHICAGO, IL 60609
P: 312.294.0501 F: 312.294.0003
PROJECT #22010109.00

ARCHITECT/ENGINEER OF RECORD
A/E:
SPEES DESIGN BUILD
23830 PACIFIC HIGHWAY S. SUITE 203
KENT, WA 98032



STAMP



Office of
Construction
and Facilities
Management



U.S. Department
of Veterans Affairs

Drawing Title
BLDG.35-36 LEVEL 01 PLAN - TECHNOLOGY

Approved:

Phase
100% CONSTRUCTION
DOCUMENTS

FULLY SPRINKLERED

Project Title
EHRM INFRASTRUCTURE
UPGRADES - HAMPTON

Location
HAMPTON VA MEDICAL CENTER, HAMPTON, VIRGINIA

Issue Date
05/09/2025

Checked
EW

Drawn
IMEG

Project Number
509-22-700
Building Number
35,36


Drawing Number
3536T-201

653 of 713


BM 360/509-22-700
VA Hampton
EHRM 35-700-655-36 T_P21.rvt
8/13/2025 1:18:06 PM

VA FORM 08 - 6231


		CONSULTANT ENGINEERING DISCIPLINE:  www.imegcorp.com 225 W WASHINGTON STREET SUITE 2700 CHICAGO, IL 60606 P: 312.294.0501 F: 312.294.0003 PROJECT #22010109.00	ARCHITECT/ENGINEER OF RECORD A/E:  SPEESDESIGNBUILD 23830 PACIFIC HIGHWAY S. SUITE 203 KENT, WA 98032	STAMP  RCDD <i>John T. Bicsi</i>	Office of Construction and Facilities Management  U.S. Department of Veterans Affairs	Drawing Title BLDG.35-36 TECHNOLOGY ENLARGEMENT PLANS Approved:	Phase 100% CONSTRUCTION DOCUMENTS FULLY SPRINKLERED	Project Title EHRM INFRASTRUCTURE UPGRADES - HAMPTON Location HAMPTON VA MEDICAL CENTER, HAMPTON, VIRGINIA Issue Date 05/09/2025	Project Number 509-22-700 Building Number 35,36 Issue Date 05/09/2025 Checked EW Drawn IMEG	Drawing Number 3536T-400 654 of 713
Revisions:		Date:								

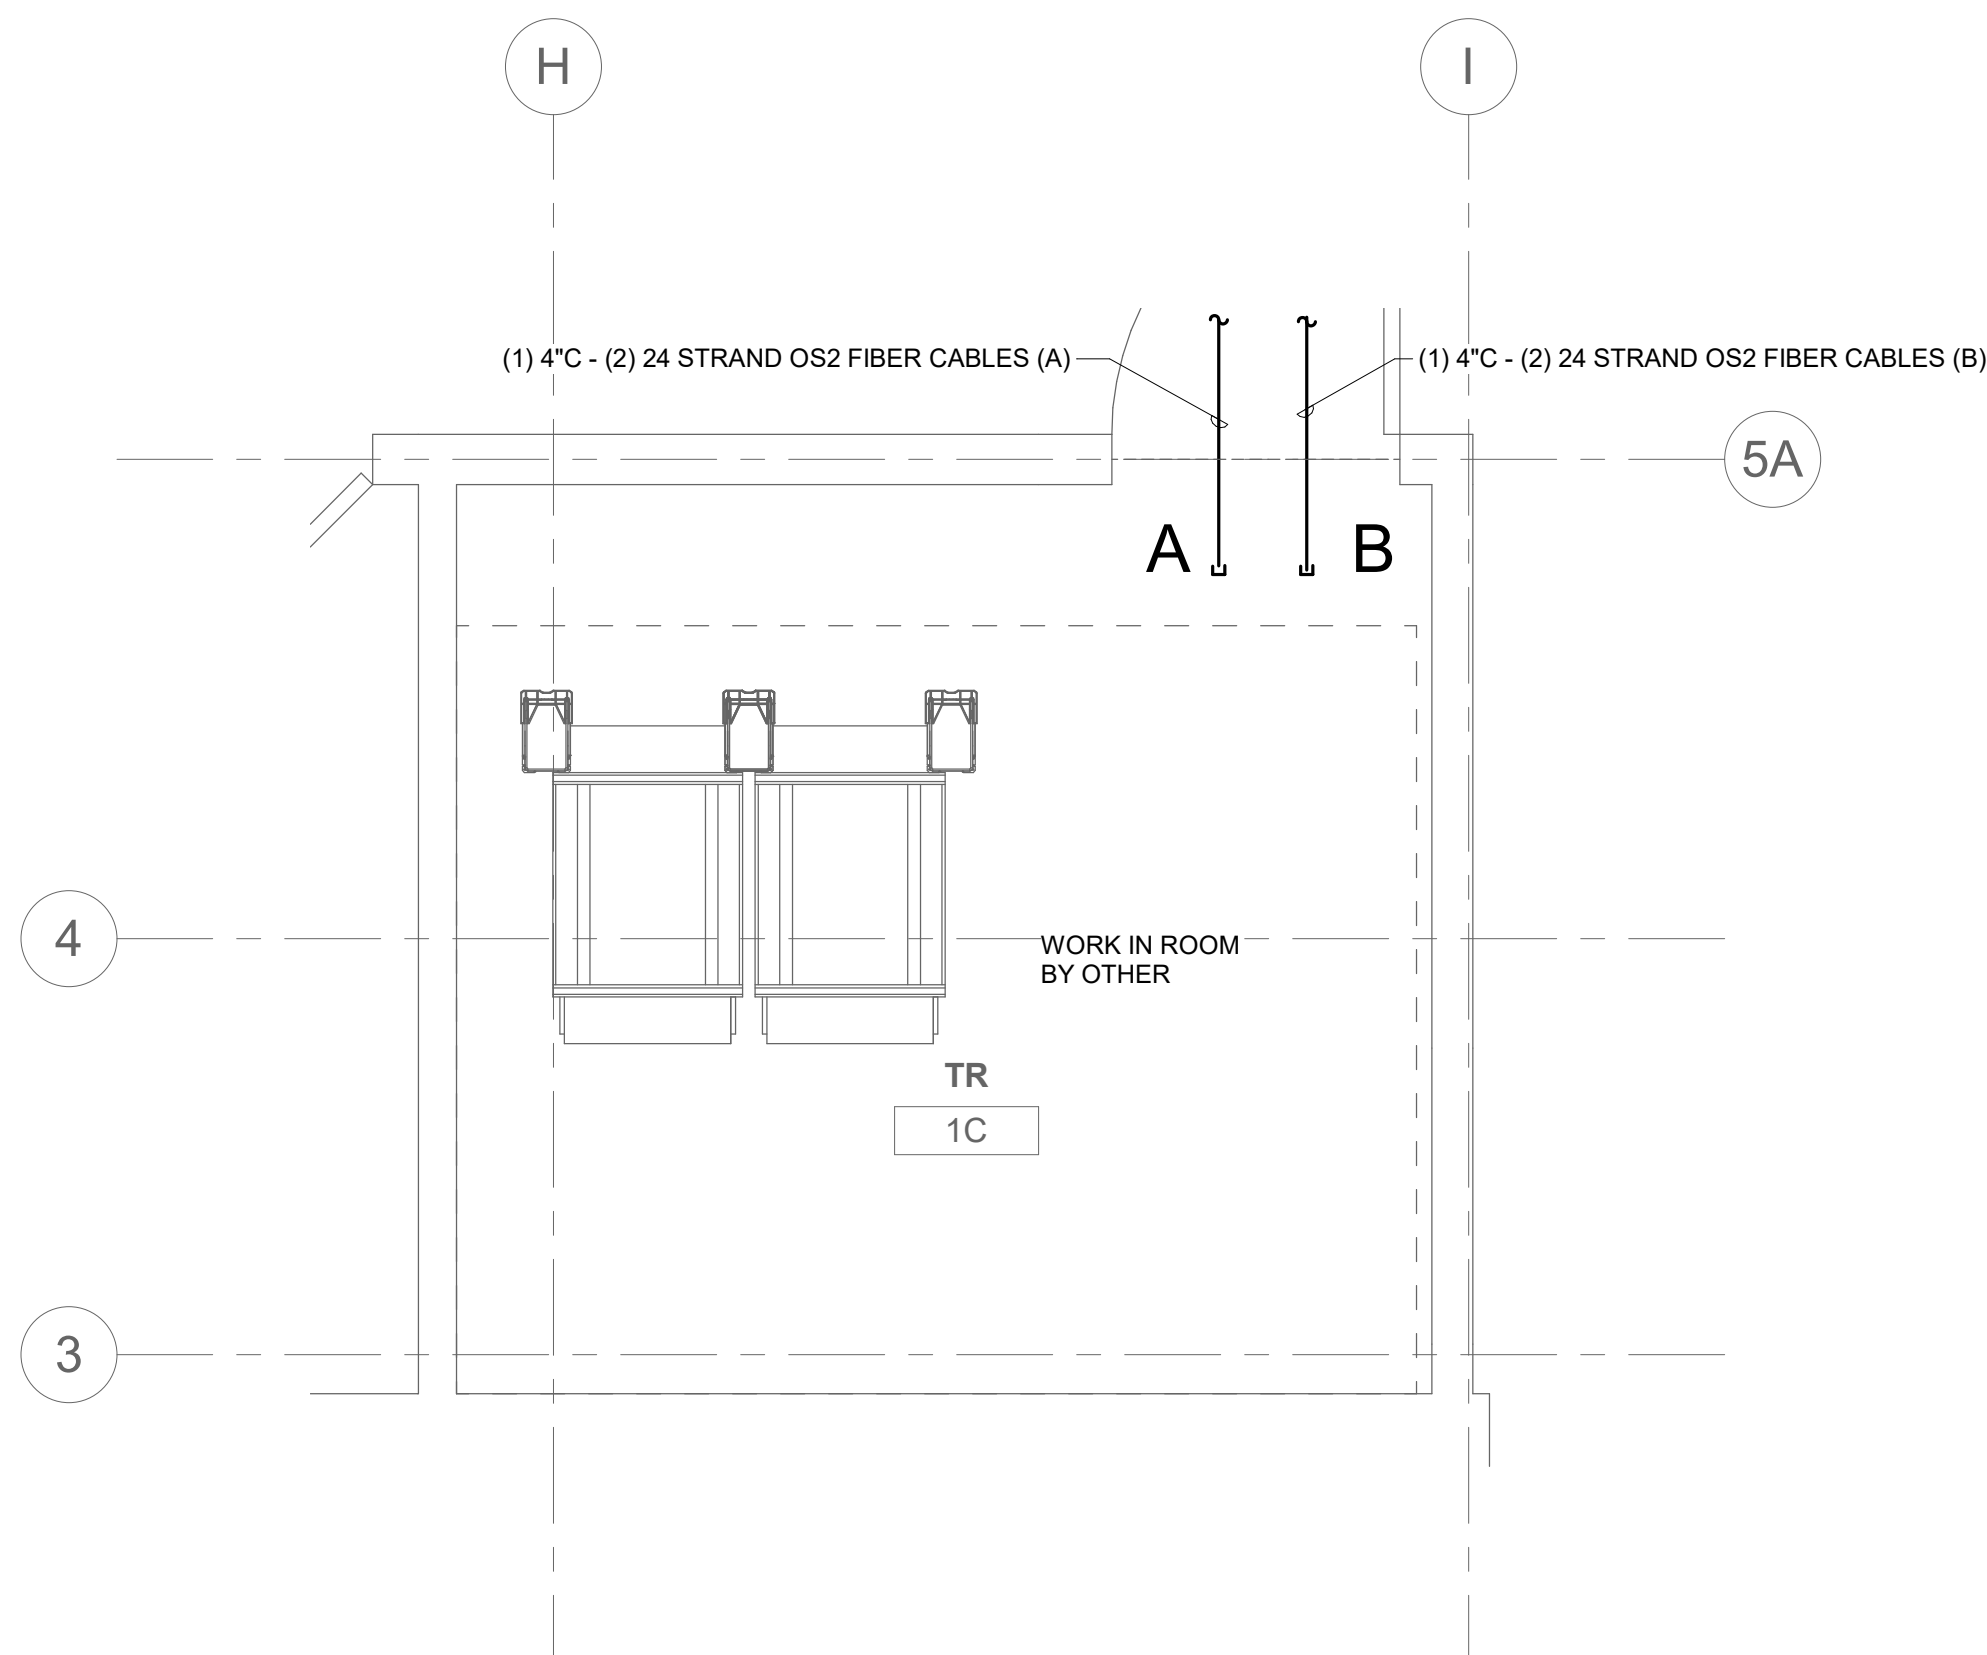

1 TELECOM ROOM ENLARGEMENT TR #36-05
1/2" = 1'-0"
NOTES:
1. REFER TO ELECTRICAL DRAWINGS FOR ROOM LAYOUT AND RACK ELEVATIONS.
2. ROUTE OPTICAL FIBER CABLE TO OVERHEAD CABLE TRAY AND TERMINATE IN FIBER DISTRIBUTION CABINET.
KEY NOTES: **#**
1. THROUGH WALL PENETRATION FOR BACKBONE CONDUIT. OPTICAL FIBER CABLE CONTINUES ON CABLE TRAY TO RACKS.

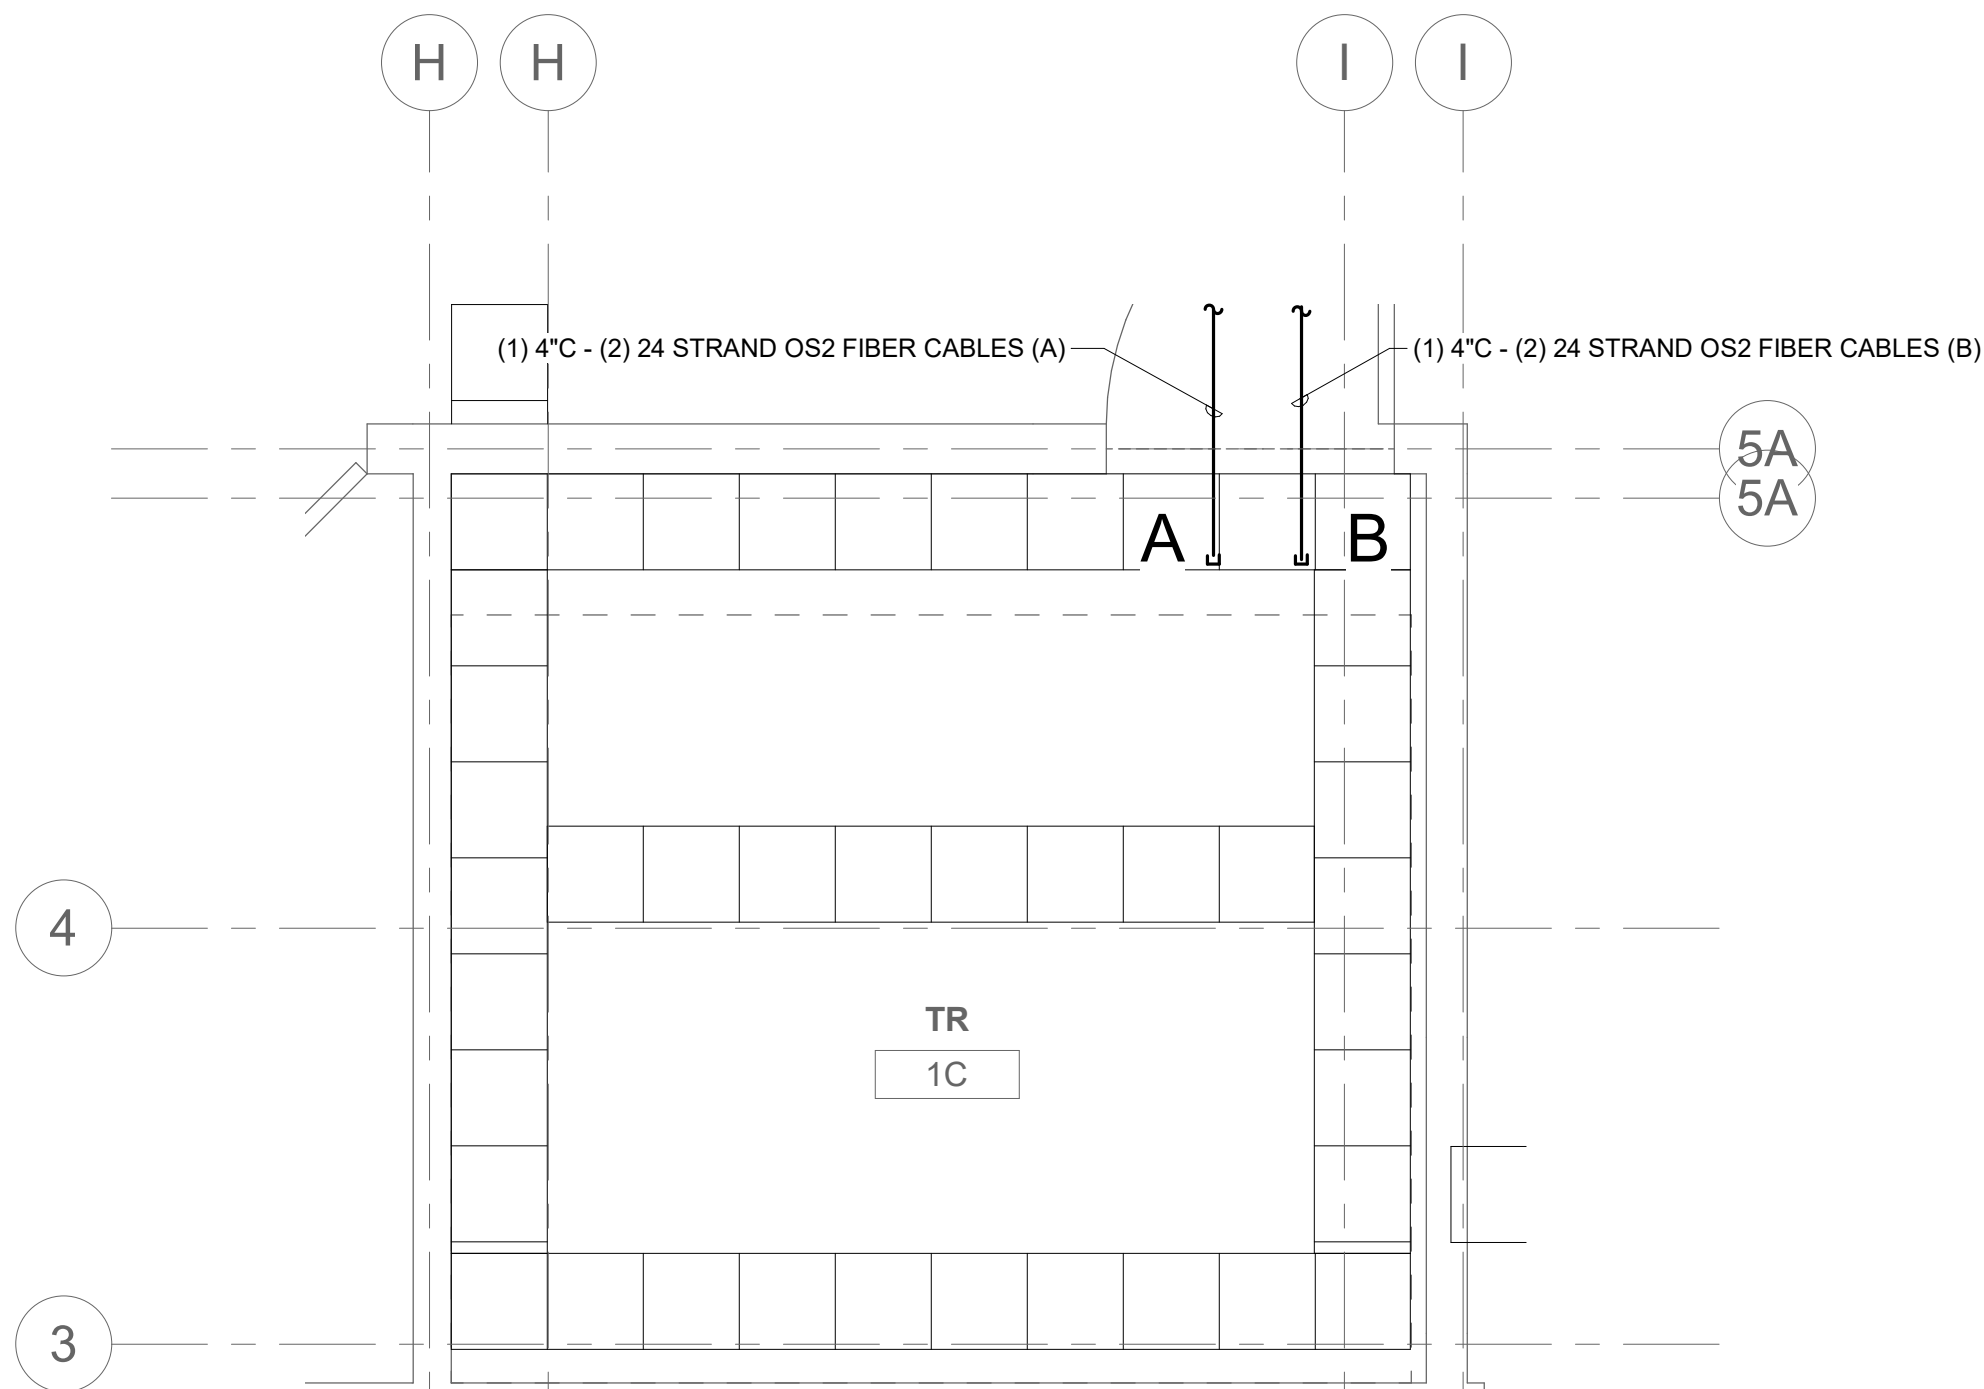


2 TELECOM ROOM PATHWAY TR #36-05
1/2" = 1'-0"

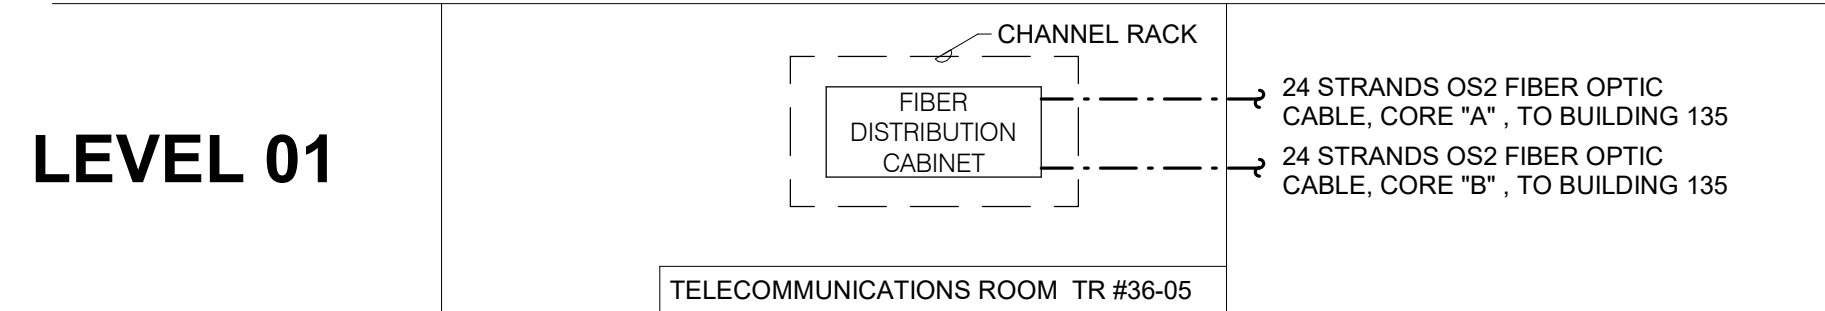

3 FIBER RISER DIAGRAM
NO SCALE
NOTES:
1. THIS RISER IS DIAGRAMMATIC AND MAY NOT SHOW ACTUAL ROUTING OR QUANTITIES OF MATERIALS SHOWN. THIS RISER IS SHOWN FOR CLARIFICATION OF CONNECTION(S), LOCATIONS AND CABLE TYPE. ALL INFORMATION OUTLETS ARE TYPICAL OF THE OUTLETS IN THE AREA SHOWN. REFER TO FLOOR PLANS FOR MORE SPECIFIC ROUTING INFORMATION. REFER TO SPECIFICATIONS FOR ADDITIONAL REQUIREMENTS.
2. REFER TO ELECTRICAL DRAWINGS FOR CHANNEL RACK AND FIBER OPTIC DISTRIBUTION CABINET SPECIFICATIONS

A
B
C
D
E
F

- SHEET NOTES:**
 - REFER TO SITEPLAN TS001 FOR ADDITIONAL INFORMATION.
 - REFER TO TS00 AND TS01 FOR CAMPUS OPTICAL FIBER CABLE RISER DIAGRAMS.
 - REFER TO 27T400 FOR HANDHOLE DETAIL.
 - NEW BACKBONE OPTICAL FIBER CABLES SHALL BE INDOOR/OUTDOOR TYPE.
 - ALL BACKBONE OPTICAL FIBER CABLE PATHWAYS SHALL BE NEW. DO NOT RE-USE EXISTING BACKBONE CABLE PATHWAYS FOR NEW BACKBONE CABLES.
 - TRANSITION PVC CONDUITS TO GRC IN CRAWL SPACE OR EXPOSED EXTERIOR LOCATIONS. TRANSITION TO EMT CONDUITS AT INTERIOR OF BUILDING. SEAL ALL PENETRATIONS TO MAINTAIN FIRE-RATINGS OF WALL, CEILING AND FLOORS.
- KEY NOTES:**
 - PROVIDE PULLBOX ON EXTERIOR WALL AT HEIGHT OF CRAWL SPACE CEILING. PROVIDE PENETRATION THRU WALL AND ROUTE CONDUIT THRU PULLBOX INTO CRAWL SPACE. CONTINUE ROUTE THRU CRAWL SPACE TO LOCATION BELOW TR #114. PROVIDE PENETRATION THRU CRAWL SPACE CEILING AND ROUTE CONDUIT UP TO ABOVE CABLE TRAY HEIGHT IN TR #114.

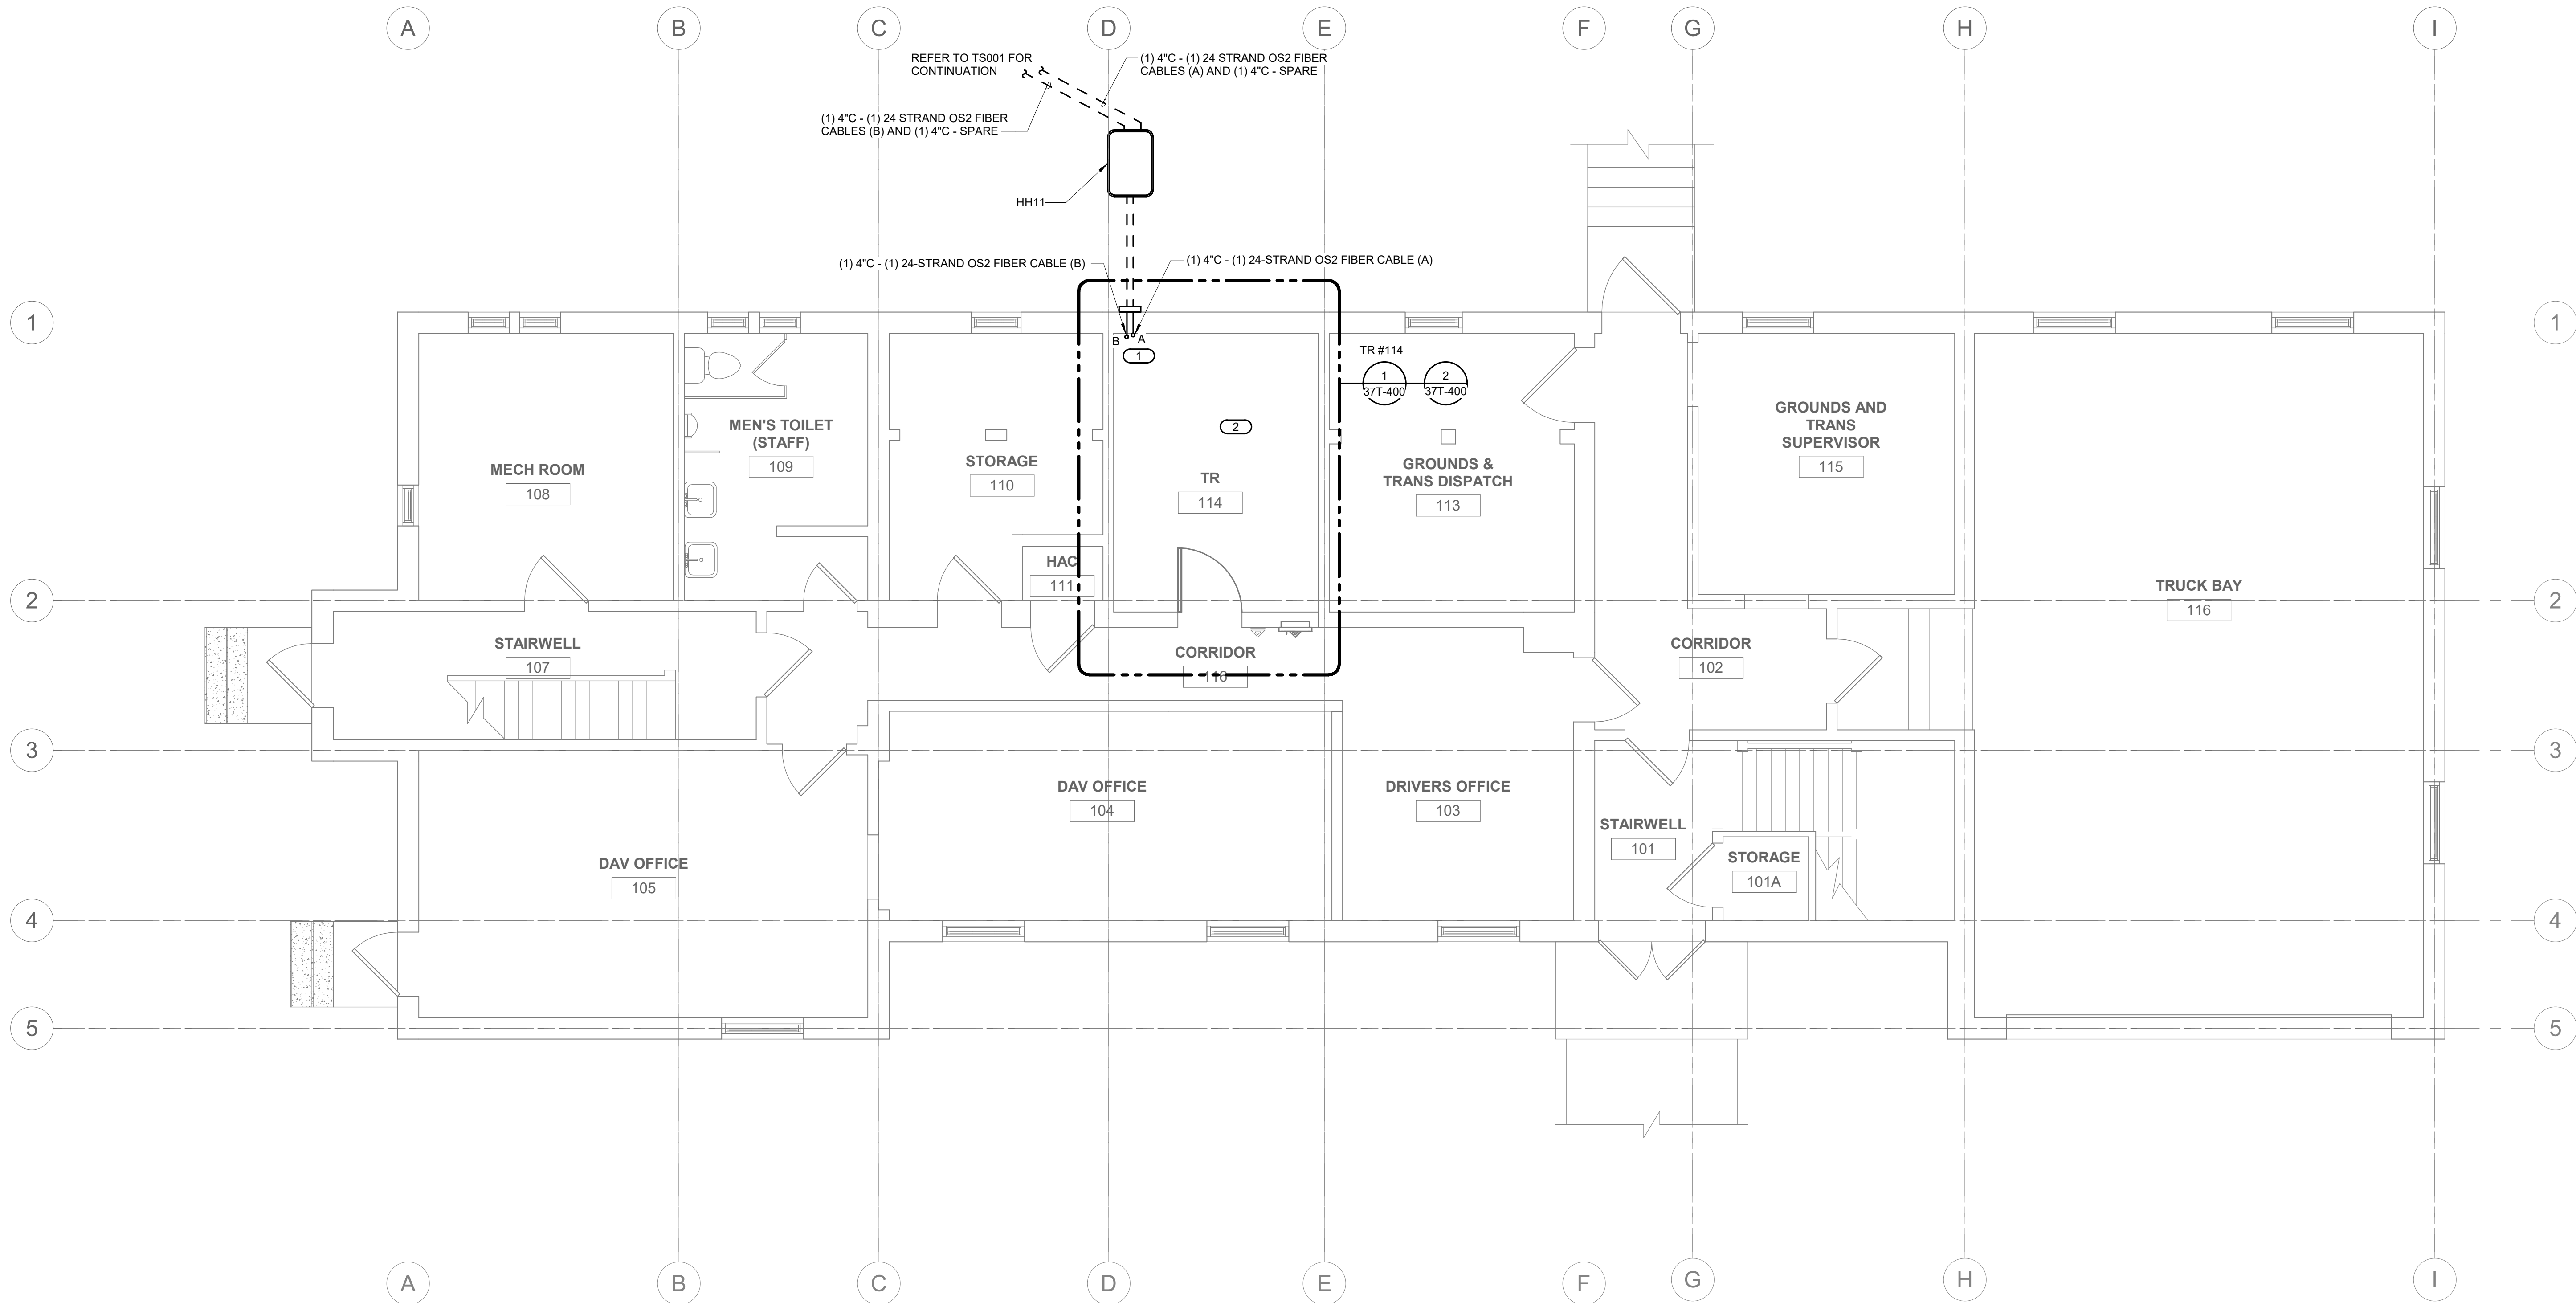

1 LEVEL 01 PLAN - TECHNOLOGY
1/4" = 1'-0"

B:\A\360\509-22-700
VAHampton
E:\A\360\509-22-700\B37.T_R21.rvt

8/21/2025 11:14:30 AM

Revisions:	
-----------------------	--	--	

A


B

C

D

E

F

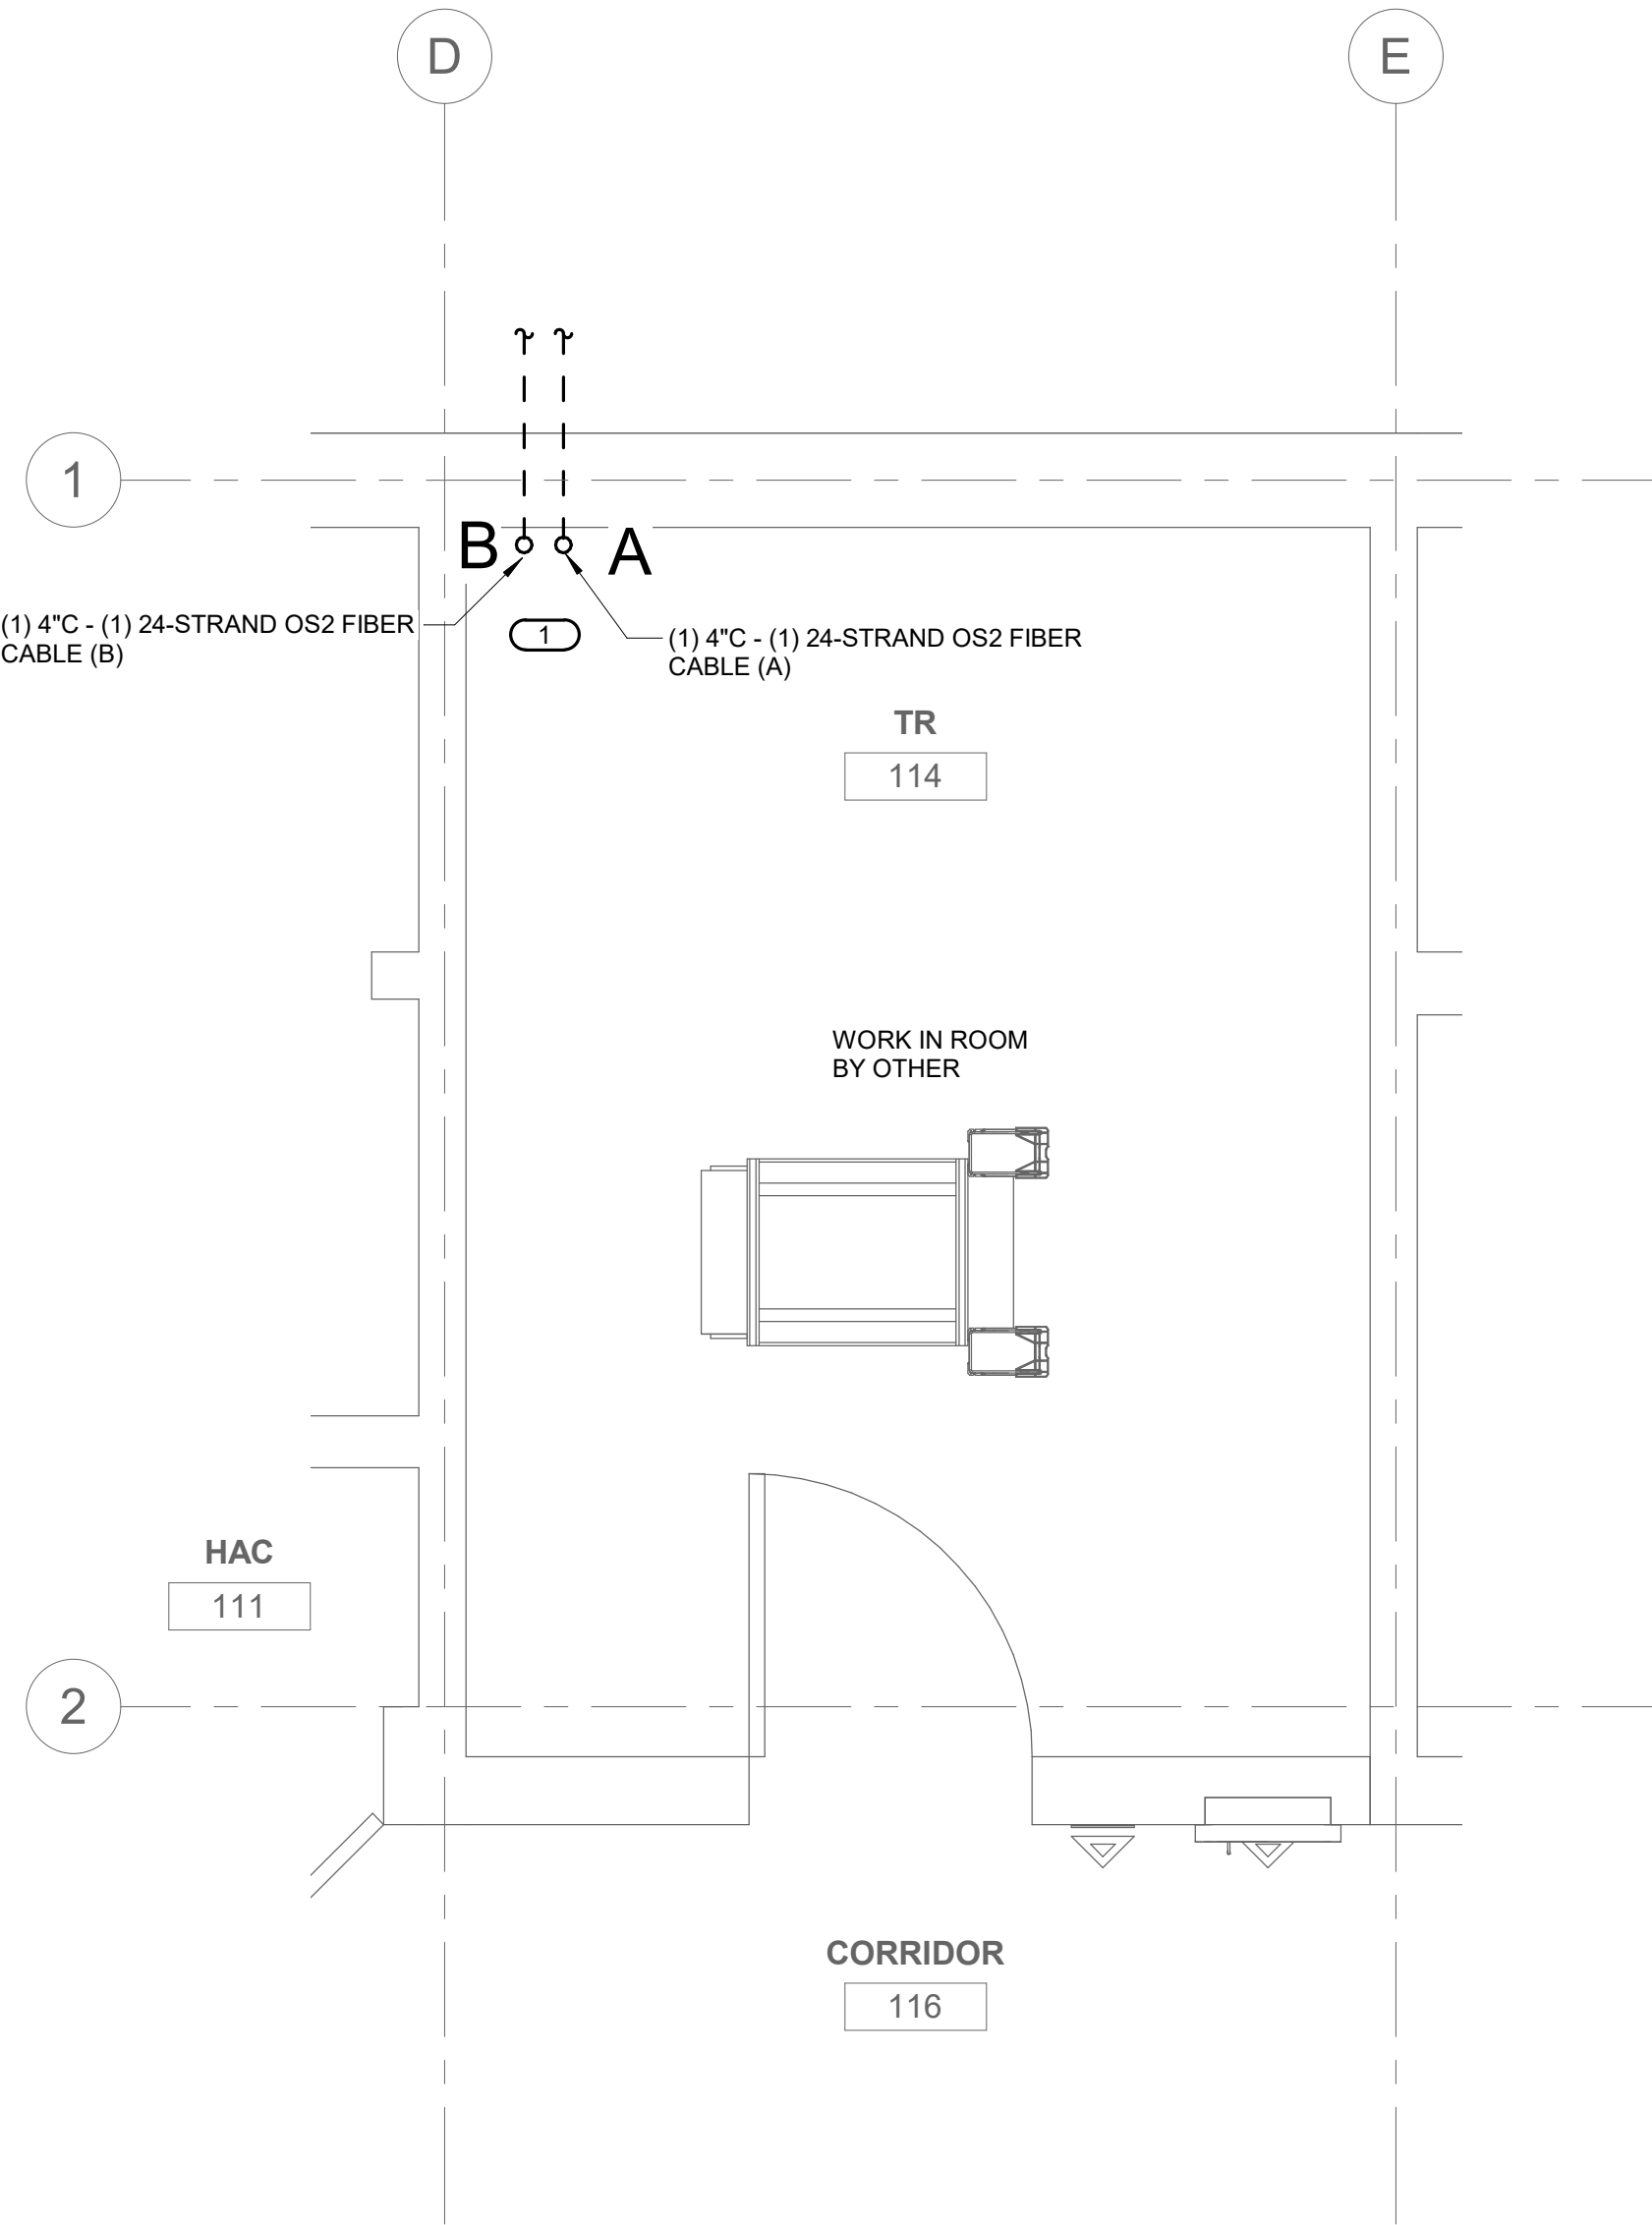

1

TELECOM ROOM ENLARGEMENT TR #114

1/2" = 1'-0"

NOTES:


1. REFER TO ELECTRICAL DRAWINGS FOR ROOM LAYOUT AND RACK ELEVATIONS.

2. ROUTE OPTICAL FIBER CABLE TO OVERHEAD CABLE TRAY AND TERMINATE IN FIBER DISTRIBUTION CABINET.

KEY NOTES:

#

1. THROUGH WALL PENETRATION FOR BACKBONE CONDUIT. OPTICAL FIBER CABLE CONTINUES ON CABLE TRAY TO RACKS.

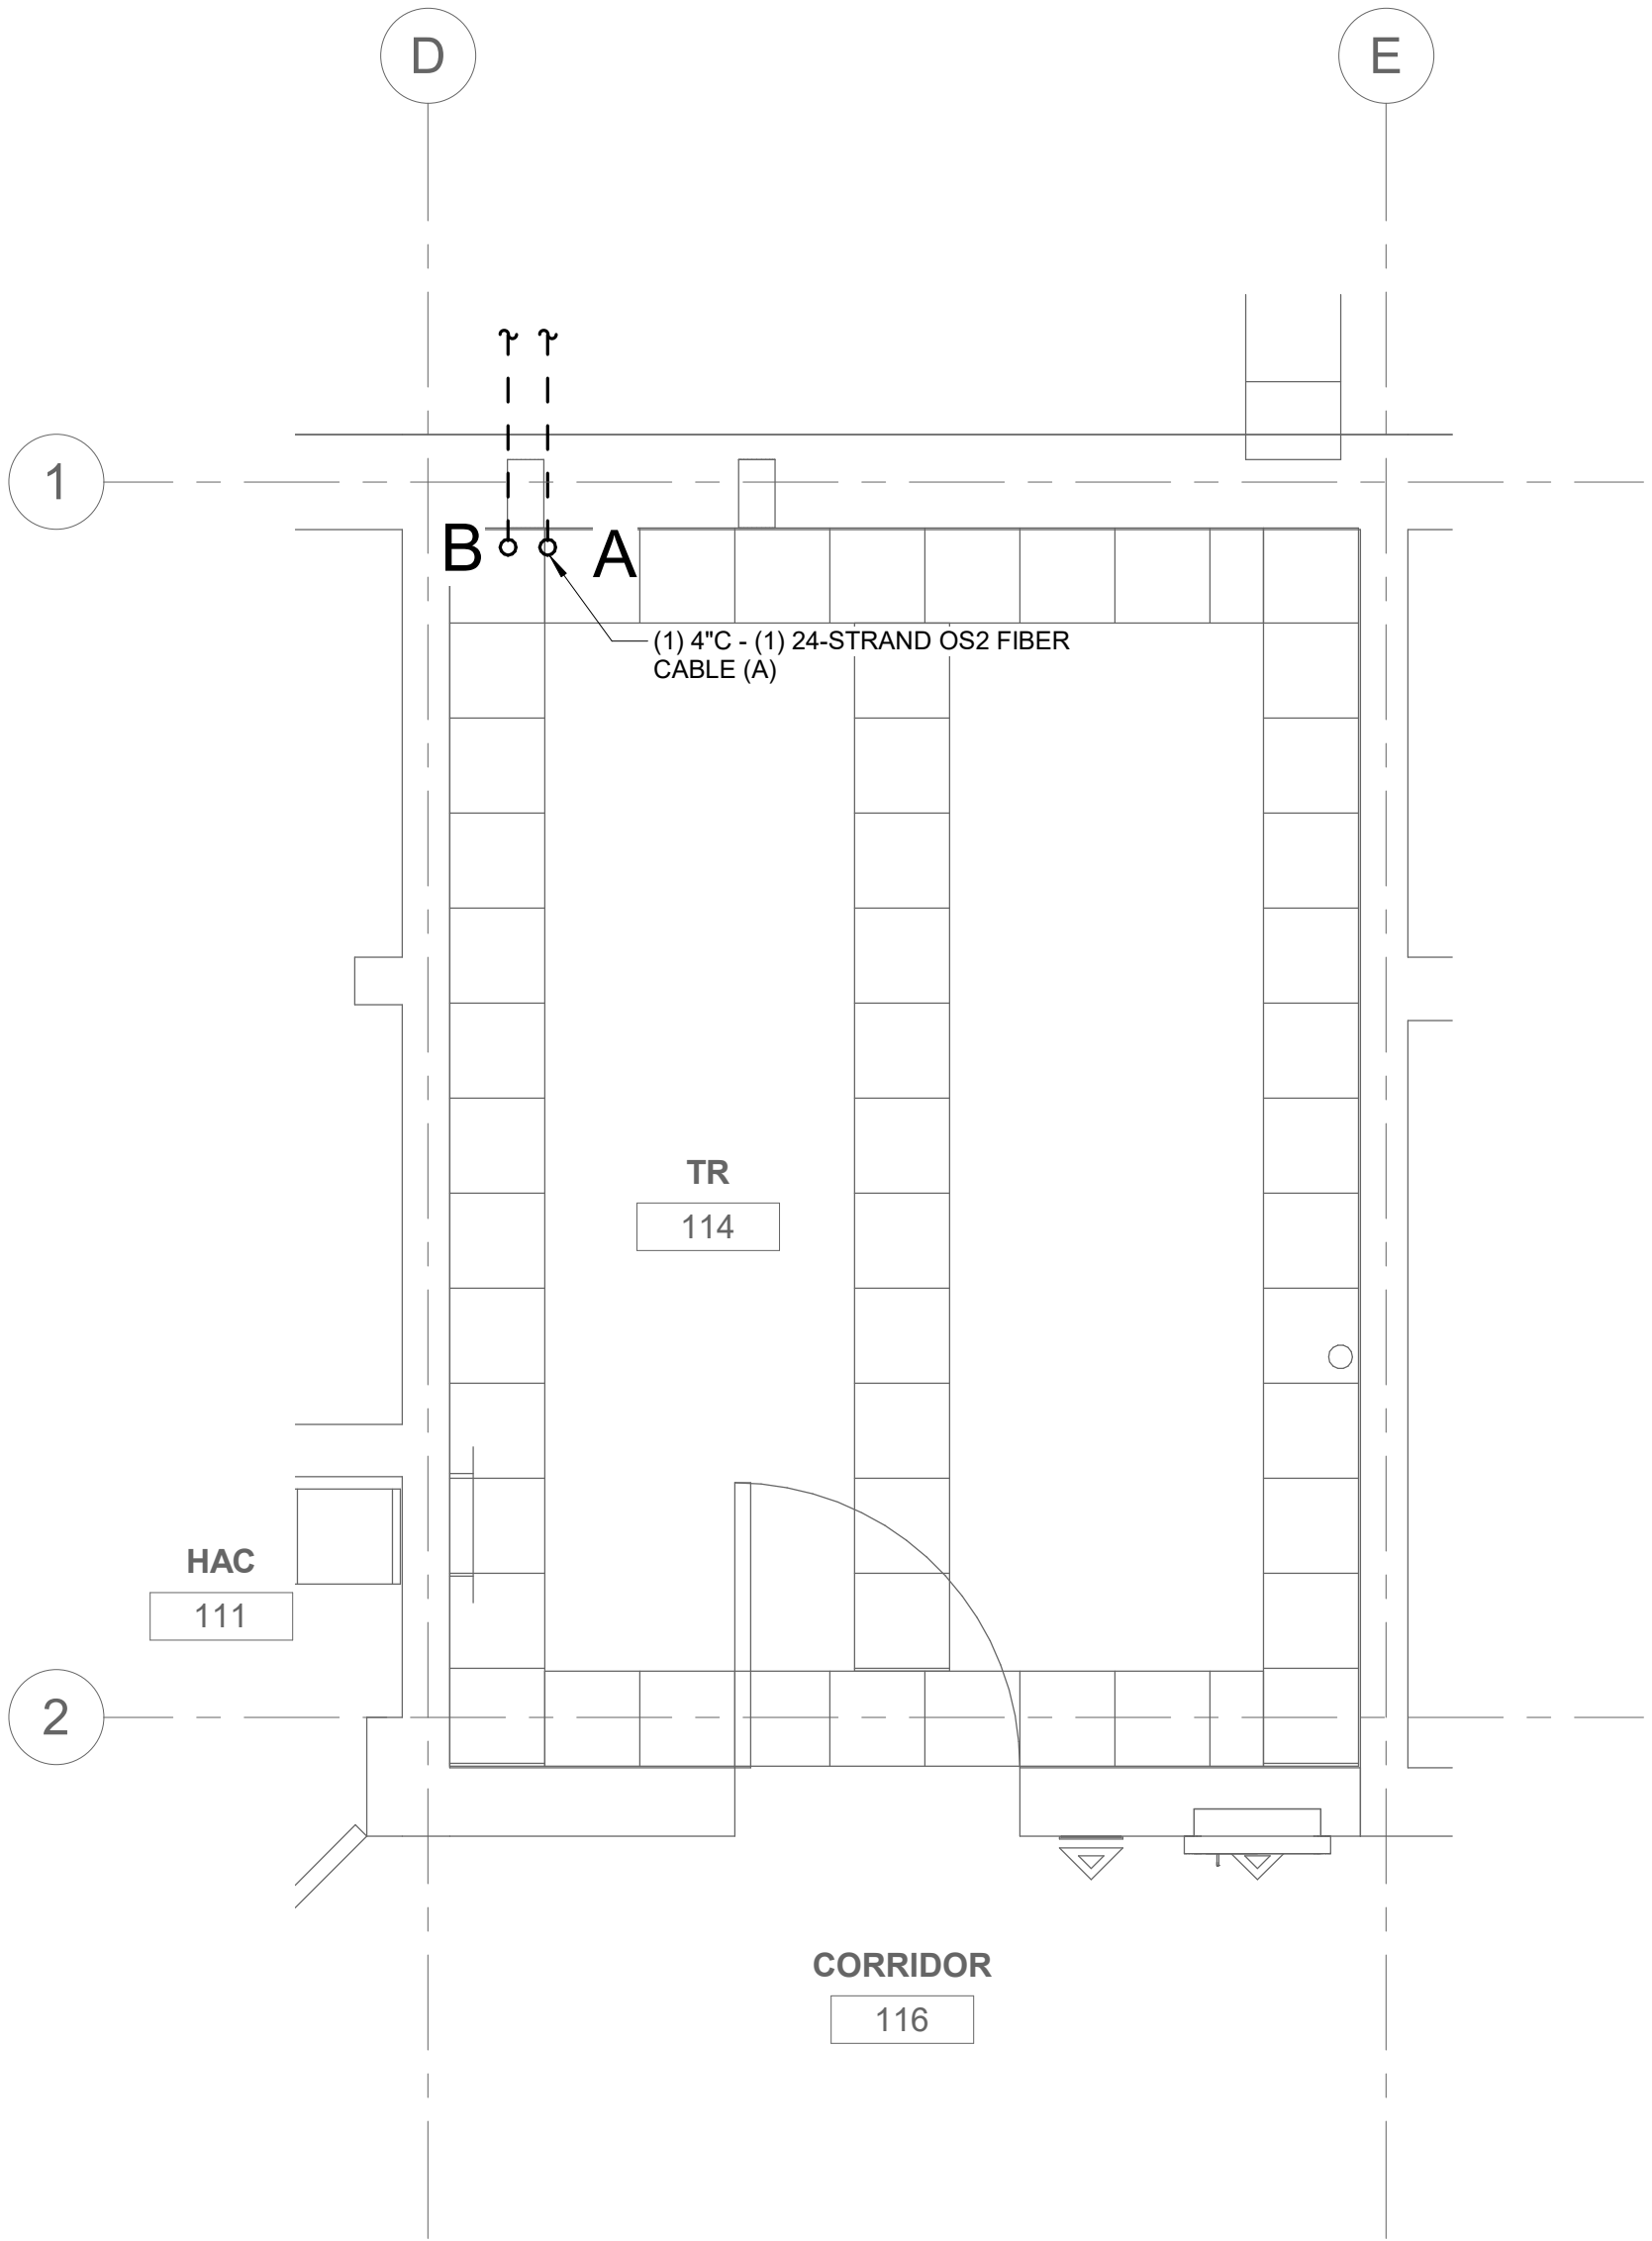


2

TELECOM ROOM PATHWAY TR #114

1/2" = 1'-0"

LEVEL 01

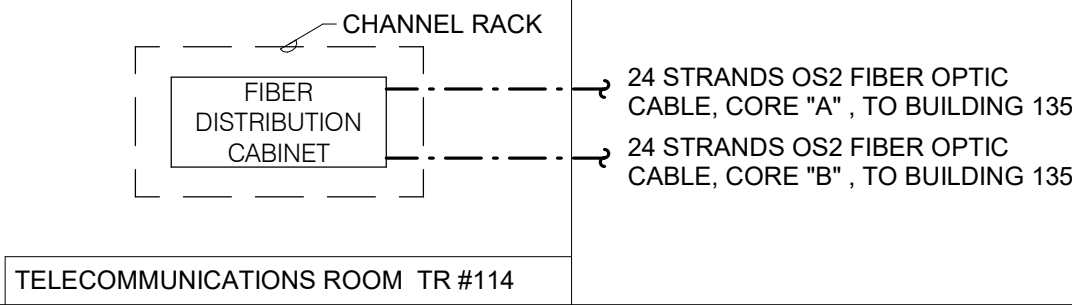

3

FIBER RISER DIAGRAM


NO SCALE

NOTES:

1. THIS RISER IS DIAGRAMMATIC AND MAY NOT SHOW ACTUAL ROUTING OR QUANTITIES OF MATERIALS SHOWN. THIS RISER IS SHOWN FOR CLARIFICATION OF CONNECTION(S), LOCATIONS AND CABLE TYPE. ALL INFORMATION OUTLETS ARE TYPICAL OF THE OUTLETS IN THE AREA SHOWN. REFER TO FLOOR PLANS FOR MORE SPECIFIC ROUTING INFORMATION. REFER TO SPECIFICATIONS FOR ADDITIONAL REQUIREMENTS.

2. REFER TO ELECTRICAL DRAWINGS FOR CHANNEL RACK AND FIBER OPTIC DISTRIBUTION CABINET SPECIFICATIONS

A
B
C
D
E
F

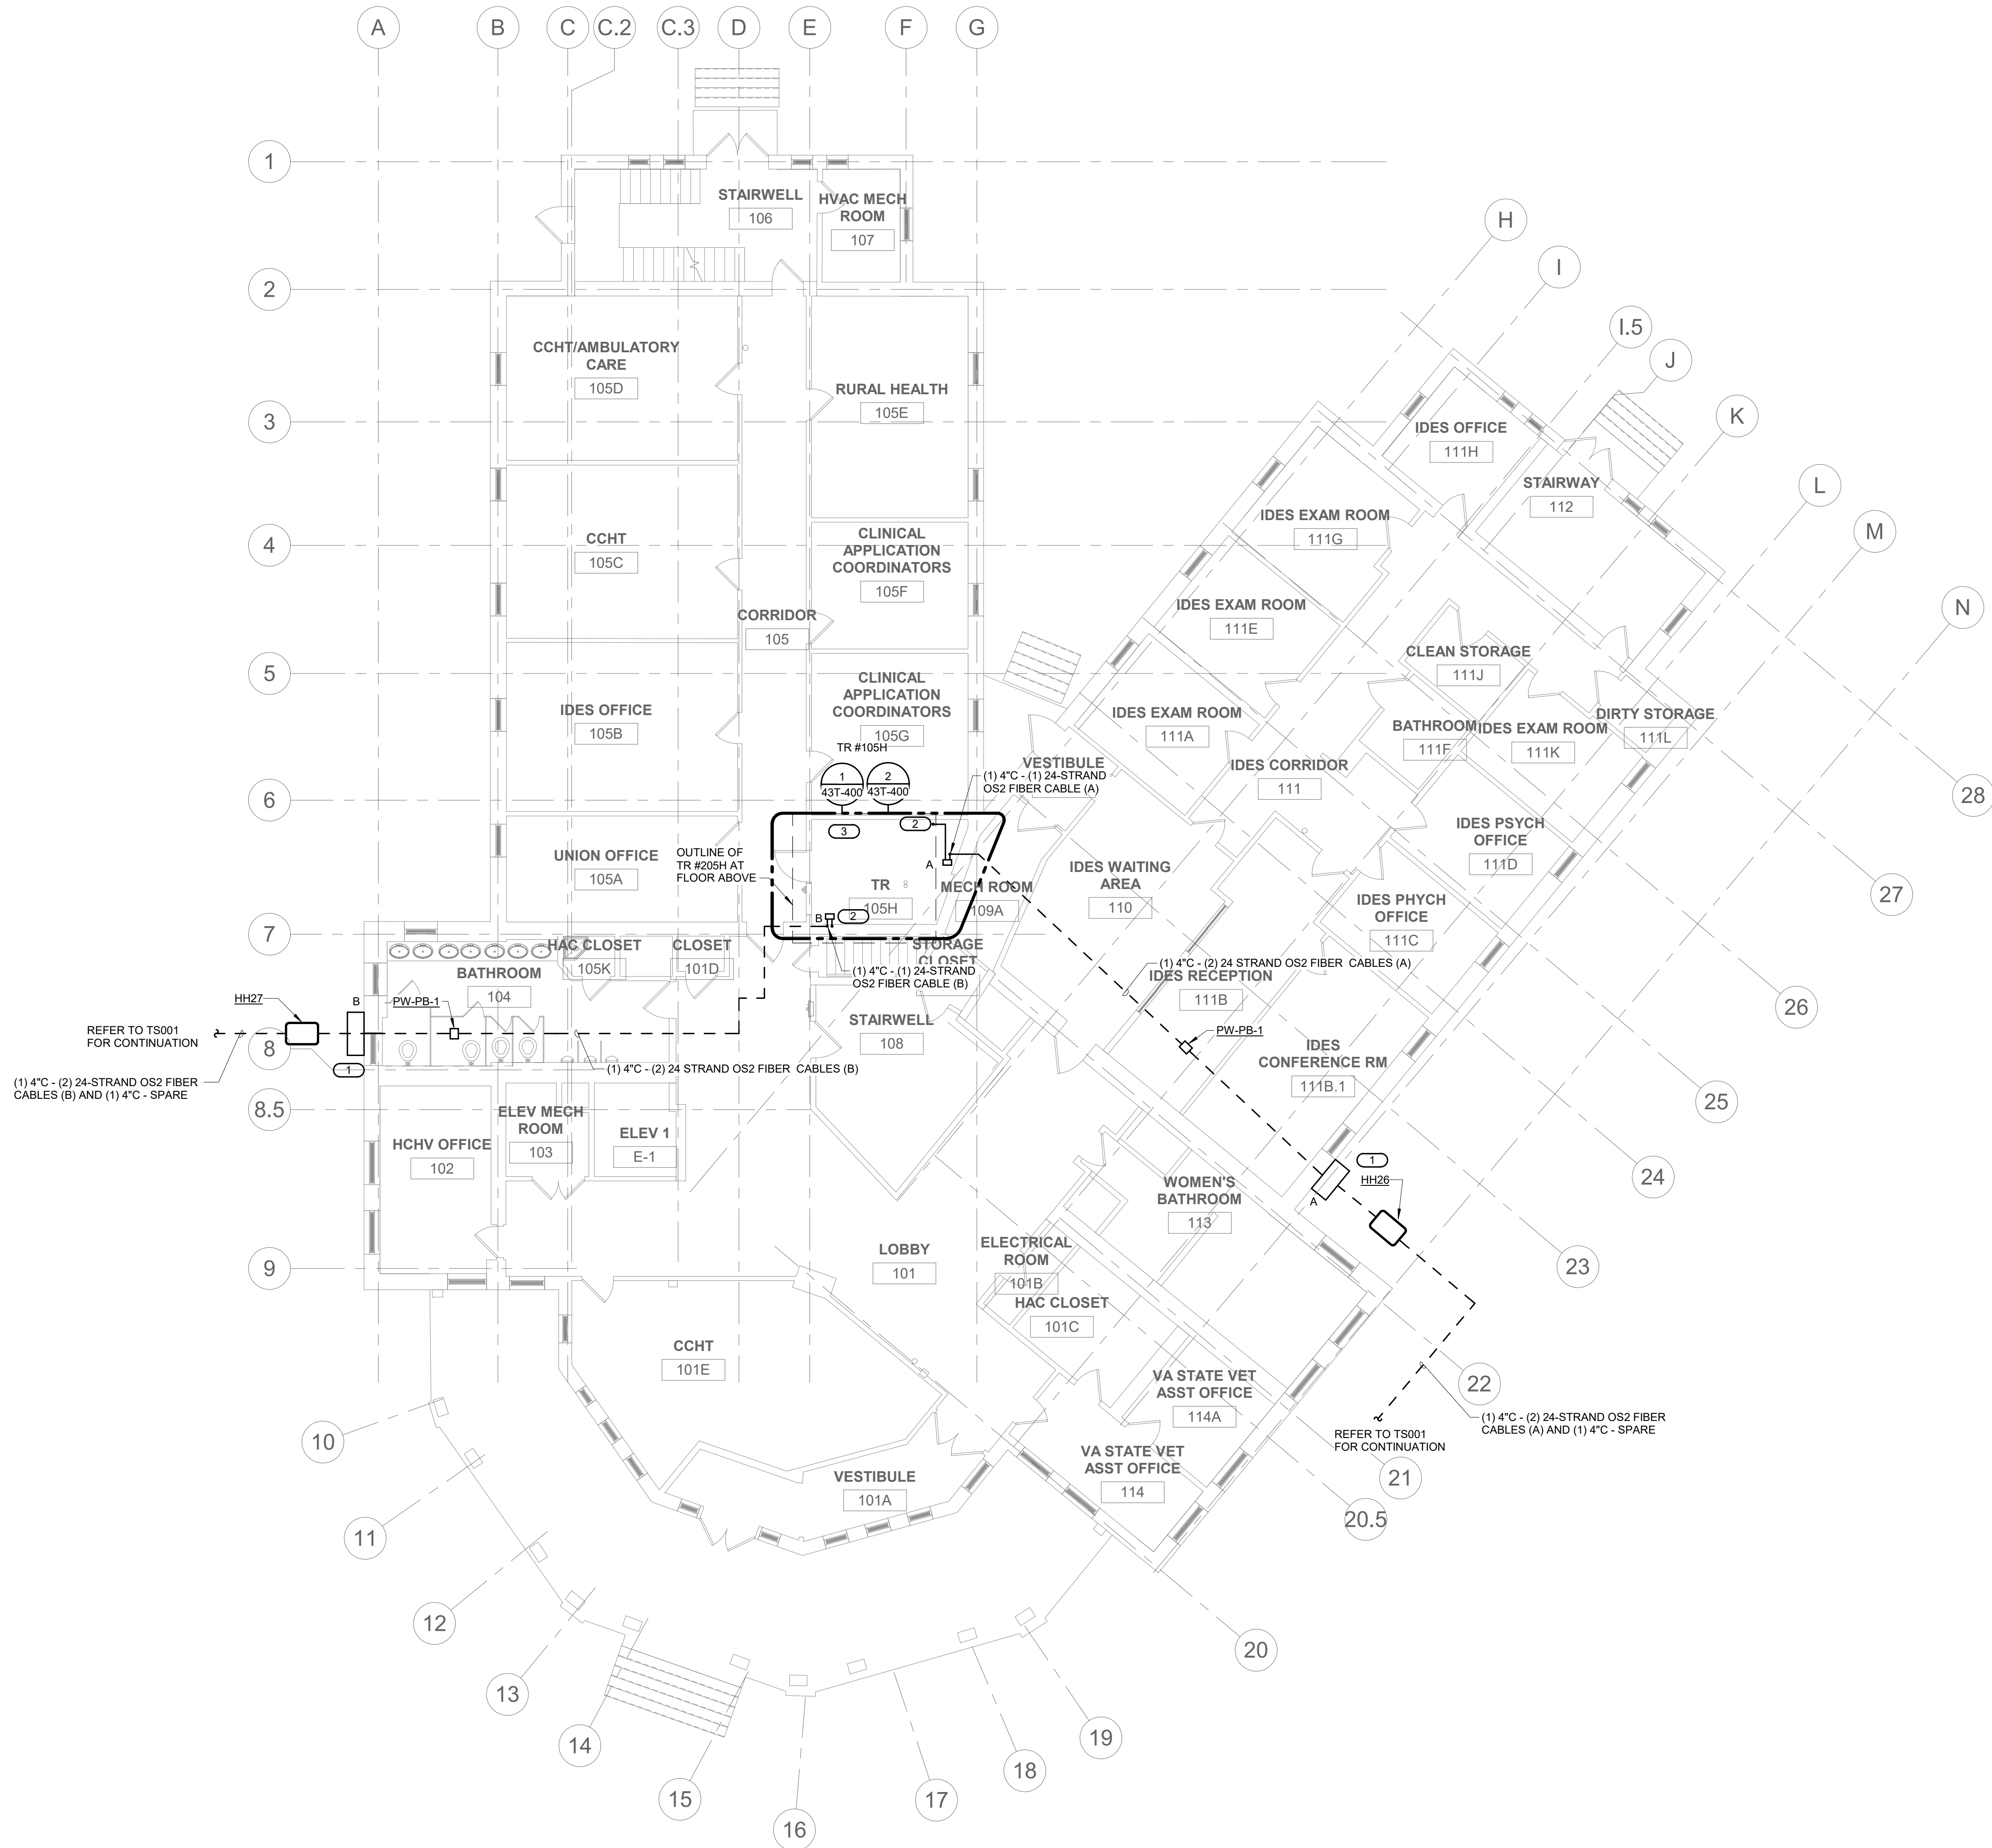

- SHEET NOTES:**
1. REFER TO SITEPLAN TS001 FOR ADDITIONAL INFORMATION.
 2. REFER TO TS00 AND TS01 FOR CAMPUS OPTICAL FIBER CABLE RISER DIAGRAMS.
 3. REFER TO 2/T400 FOR HANDHOLE DETAIL.
 4. NEW BACKBONE OPTICAL FIBER CABLES SHALL BE INDOOR/OUTDOOR TYPE.
 5. ALL BACKBONE OPTICAL FIBER CABLE PATHWAYS SHALL BE NEW. DO NOT RE-USE EXISTING BACKBONE CABLE PATHWAYS FOR NEW BACKBONE CABLES.
 6. TRANSITION PVC CONDUITS TO GRC IN CRAWL SPACE OR EXPOSED EXTERIOR LOCATIONS. TRANSITION TO EMT CONDUITS AT INTERIOR OF BUILDING. SEAL ALL PENETRATIONS TO MAINTAIN FIRE-RATINGS OF WALL, CEILING AND FLOORS.
 7. CONDUIT ROUTES THRU CRAWL SPACE ARE "SUGGESTED" ROUTE. FIELD VERIFY EXACT ROUTE THRU CRAWL SPACE.
- KEY NOTES: (C #)**
1. PROVIDE PENETRATION THRU WALL AND ROUTE CONDUIT INTO CRAWL SPACE AND CONTINUE TO LOCATION BELOW TR #105H.
 2. PROVIDE PENETRATION THRU CEILING DECK AND ROUTE CONDUIT UP INTO TR #105H.
 3. ROUTE CONDUIT UP TO HEIGHT ABOVE CABLE TRAY. PROVIDE PULLBOX AND PENETRATION THRU CEILING TO ROUTE CONDUIT UP INTO TR #205H.

1 LEVEL 01 PLAN - TECHNOLOGY
1/8" = 1'-0"

Revisions:	Date:	CONSULTANT ENGINEERING DISCIPLINE: IMEG www.imeg.com 225 W WASHINGTON STREET SUITE 2700 CHICAGO, IL 60606 P: 312.294.0501 F: 312.294.0003 PROJECT #22010109.00	ARCHITECT/ENGINEER OF RECORD A/E: SDB SPEESDESIGNBUILD SPEES DESIGN BUILD 23830 PACIFIC HIGHWAY S. SUITE 203 KENT, WA 98032	STAMP Bicsi Esde C. Wile, Jr. Reg. No. 191902R Expires 03/01/2025 RCDD	Office of Construction and Facilities Management VA U.S. Department of Veterans Affairs	Drawing Title BLDG.43 LEVEL 01 PLAN - TECHNOLOGY	Phase 100% CONSTRUCTION DOCUMENTS	Project Title EHRM INFRASTRUCTURE UPGRADES - HAMPTON	Project Number 509-22-700	
									Building Number 43	
								FULLY SPRINKLERED	Location HAMPTON VA MEDICAL CENTER, HAMPTON, VIRGINIA	Drawing Number 43T-201
									Issue Date 05/09/2025	Checked EW

BM 360/509-22-700
VA Hampton
EHRM 509-22-700 B43.T_021.rvt

8/13/2025 1:24:50 PM

VA FORM 08 - 6231

Revisions:	Date:

CONSULTANT

ENGINEERING DISCIPLINE:


www.imeg.com
225 W WASHINGTON STREET
SUITE 2700
CHICAGO, IL 60609
P: 312.294.0501 F: 312.294.0003
PROJECT #22010109.00

ARCHITECT/ENGINEER OF RECORD

A/E:

SPEES DESIGN BUILD
23830 PACIFIC HIGHWAY S, SUITE 203
KENT, WA 98032

 SPEESDESIGNBUILD

STAMP



Office of
Construction
and Facilities
Management

 U.S. Department
of Veterans Affairs

Drawing Title

BLDG.43 TECHNOLOGY ENLARGEMENTS

Approved:

Phase

100% CONSTRUCTION
DOCUMENTS

FULLY SPRINKLERED

Project Title

EHRM INFRASTRUCTURE
UPGRADES - HAMPTON

Location

HAMPTON VA MEDICAL CENTER, HAMPTON, VIRGINIA

Issue Date

05/09/2025

Checked

EW

Drawn

IMEG

Project Number

509-22-700

Building Number

43

Drawing Number

43T-400

659 of 713



1

TELECOM ROOM ENLARGEMENT TR #105H

1/2" = 1'-0"

NOTES:

- REFER TO ELECTRICAL DRAWINGS FOR ROOM LAYOUT AND RACK ELEVATIONS.
- ROUTE OPTICAL FIBER CABLE TO OVERHEAD CABLE TRAY AND TERMINATE IN FIBER DISTRIBUTION CABINET.

KEY NOTES: (B)

- THROUGH FLOOR PENETRATION FOR BACKBONE CONDUIT. OPTICAL FIBER CABLE CONTINUES ON CABLE TRAY TO RACKS.



2

TELECOM ROOM PATHWAY TR #105H

1/2" = 1'-0"

3

FIBER RISER DIAGRAM

NO SCALE

NOTES:

- THIS RISER IS DIAGRAMMATIC AND MAY NOT SHOW ACTUAL ROUTING OR QUANTITIES OF MATERIALS SHOWN. THIS RISER IS SHOWN FOR CLARIFICATION OF CONNECTION(S), LOCATIONS AND CABLE TYPE. ALL INFORMATION OUTLETS ARE TYPICAL OF THE OUTLETS IN THE AREA SHOWN. REFER TO FLOOR PLANS FOR MORE SPECIFIC ROUTING INFORMATION. REFER TO SPECIFICATIONS FOR ADDITIONAL REQUIREMENTS.
- REFER TO ELECTRICAL DRAWINGS FOR CHANNEL RACK AND FIBER OPTIC DISTRIBUTION CABINET SPECIFICATIONS



4

TELECOM ROOM ENLARGEMENT TR #205H

1/2" = 1'-0"

NOTES:

- REFER TO ELECTRICAL DRAWINGS FOR ROOM LAYOUT AND RACK ELEVATIONS.
- ROUTE OPTICAL FIBER CABLE TO OVERHEAD CABLE TRAY AND TERMINATE IN FIBER DISTRIBUTION CABINET.

KEY NOTES: (B)



- THROUGH FLOOR/CEILING PENETRATION FOR BACKBONE CONDUIT. CONDUIT SHALL CONTINUE UP TO HEIGHT OF CABLE TRAY. OPTICAL FIBER CABLE CONTINUES ON CABLE TRAY TO RACKS.
- PROVIDE NEW PATHWAY THRU WALL OF TELECOM ROOM TO ROUTE FIBER CABLES INTO COMPUTER ROOM #209A.
- PROVIDE (2) SETS OF 2-STRAND, OMA, OPTICAL FIBER CABLES FROM CORE A AND CORE B IN FIBER DISTRIBUTION CABINET IN NEW RACK TO EXISTING NETWORK SWITCHES IN COMPUTER LAB #209A VIA INNERDUCT AND CABLE SUPPORTS. TERMINATE BOTH ENDS OF EACH CABLE WITH LC CONNECTORS. REFER TO SECOND FLOOR PLAN FOR LOCATION OF COMPUTER LAB #209A.



5


TELECOM ROOM PATHWAY TR #205H

1/2" = 1'-0"

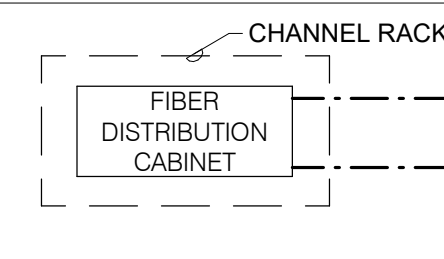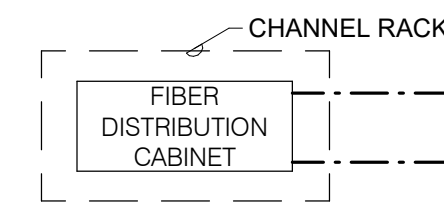LEVEL 02		24 STRANDS OS2 FIBER OPTIC CABLE, CORE "A", TO BUILDING 135 24 STRANDS OS2 FIBER OPTIC CABLE, CORE "B", TO BUILDING 135
	TELECOMMUNICATIONS ROOM TR #205H	
LEVEL 01		24 STRANDS OS2 FIBER OPTIC CABLE, CORE "A", TO BUILDING 135 24 STRANDS OS2 FIBER OPTIC CABLE, CORE "B", TO BUILDING 135
	TELECOMMUNICATIONS ROOM TR #105H	

- SHEET NOTES:**
1. REFER TO SITEPLAN TS001 FOR ADDITIONAL INFORMATION.
 2. REFER TO TS00 AND TS01 FOR CAMPUS OPTICAL FIBER CABLE RISER DIAGRAMS.
 3. REFER TO 2/T400 FOR HANDHOLE DETAIL.
 4. NEW BACKBONE OPTICAL FIBER CABLES SHALL BE INDOOR/OUTDOOR TYPE.
 5. ALL BACKBONE OPTICAL FIBER CABLE PATHWAYS SHALL BE NEW. DO NOT RE-USE EXISTING BACKBONE CABLE PATHWAYS FOR NEW BACKBONE CABLES.
 6. TRANSITION PVC CONDUITS TO GRC IN CRAWL SPACE OR EXPOSED EXTERIOR LOCATIONS. TRANSITION TO EMT CONDUITS AT INTERIOR OF BUILDING. SEAL ALL PENETRATIONS TO MAINTAIN FIRE-RATINGS OF WALL, CEILING AND FLOORS.

- KEYNOTES:** C #
1. PROVIDE PULLBOX ON EXTERIOR WALL AT HEIGHT OF FIRST FLOOR CEILING. ROUTE CONDUIT FROM HANDHOLE UP WALL INTO PULLBOX. PROVIDE PENETRATIONS THRU WALLS AND CONTINUE ROUTE ABOVE. CORRIDOR FINISHED CEILING OVER INTO TR #105.
 2. ROUTE CONDUITS INTO TR #105 AT ABOVE HEIGHT OF CABLE TRAY. PROVIDE PULLBOX AND ROUTE CONDUIT TO LOCATION BELOW TR #202. PROVIDE PENETRATIONS THRU CEILING DECK AND ROUTE CONDUITS UP INTO TR #202.

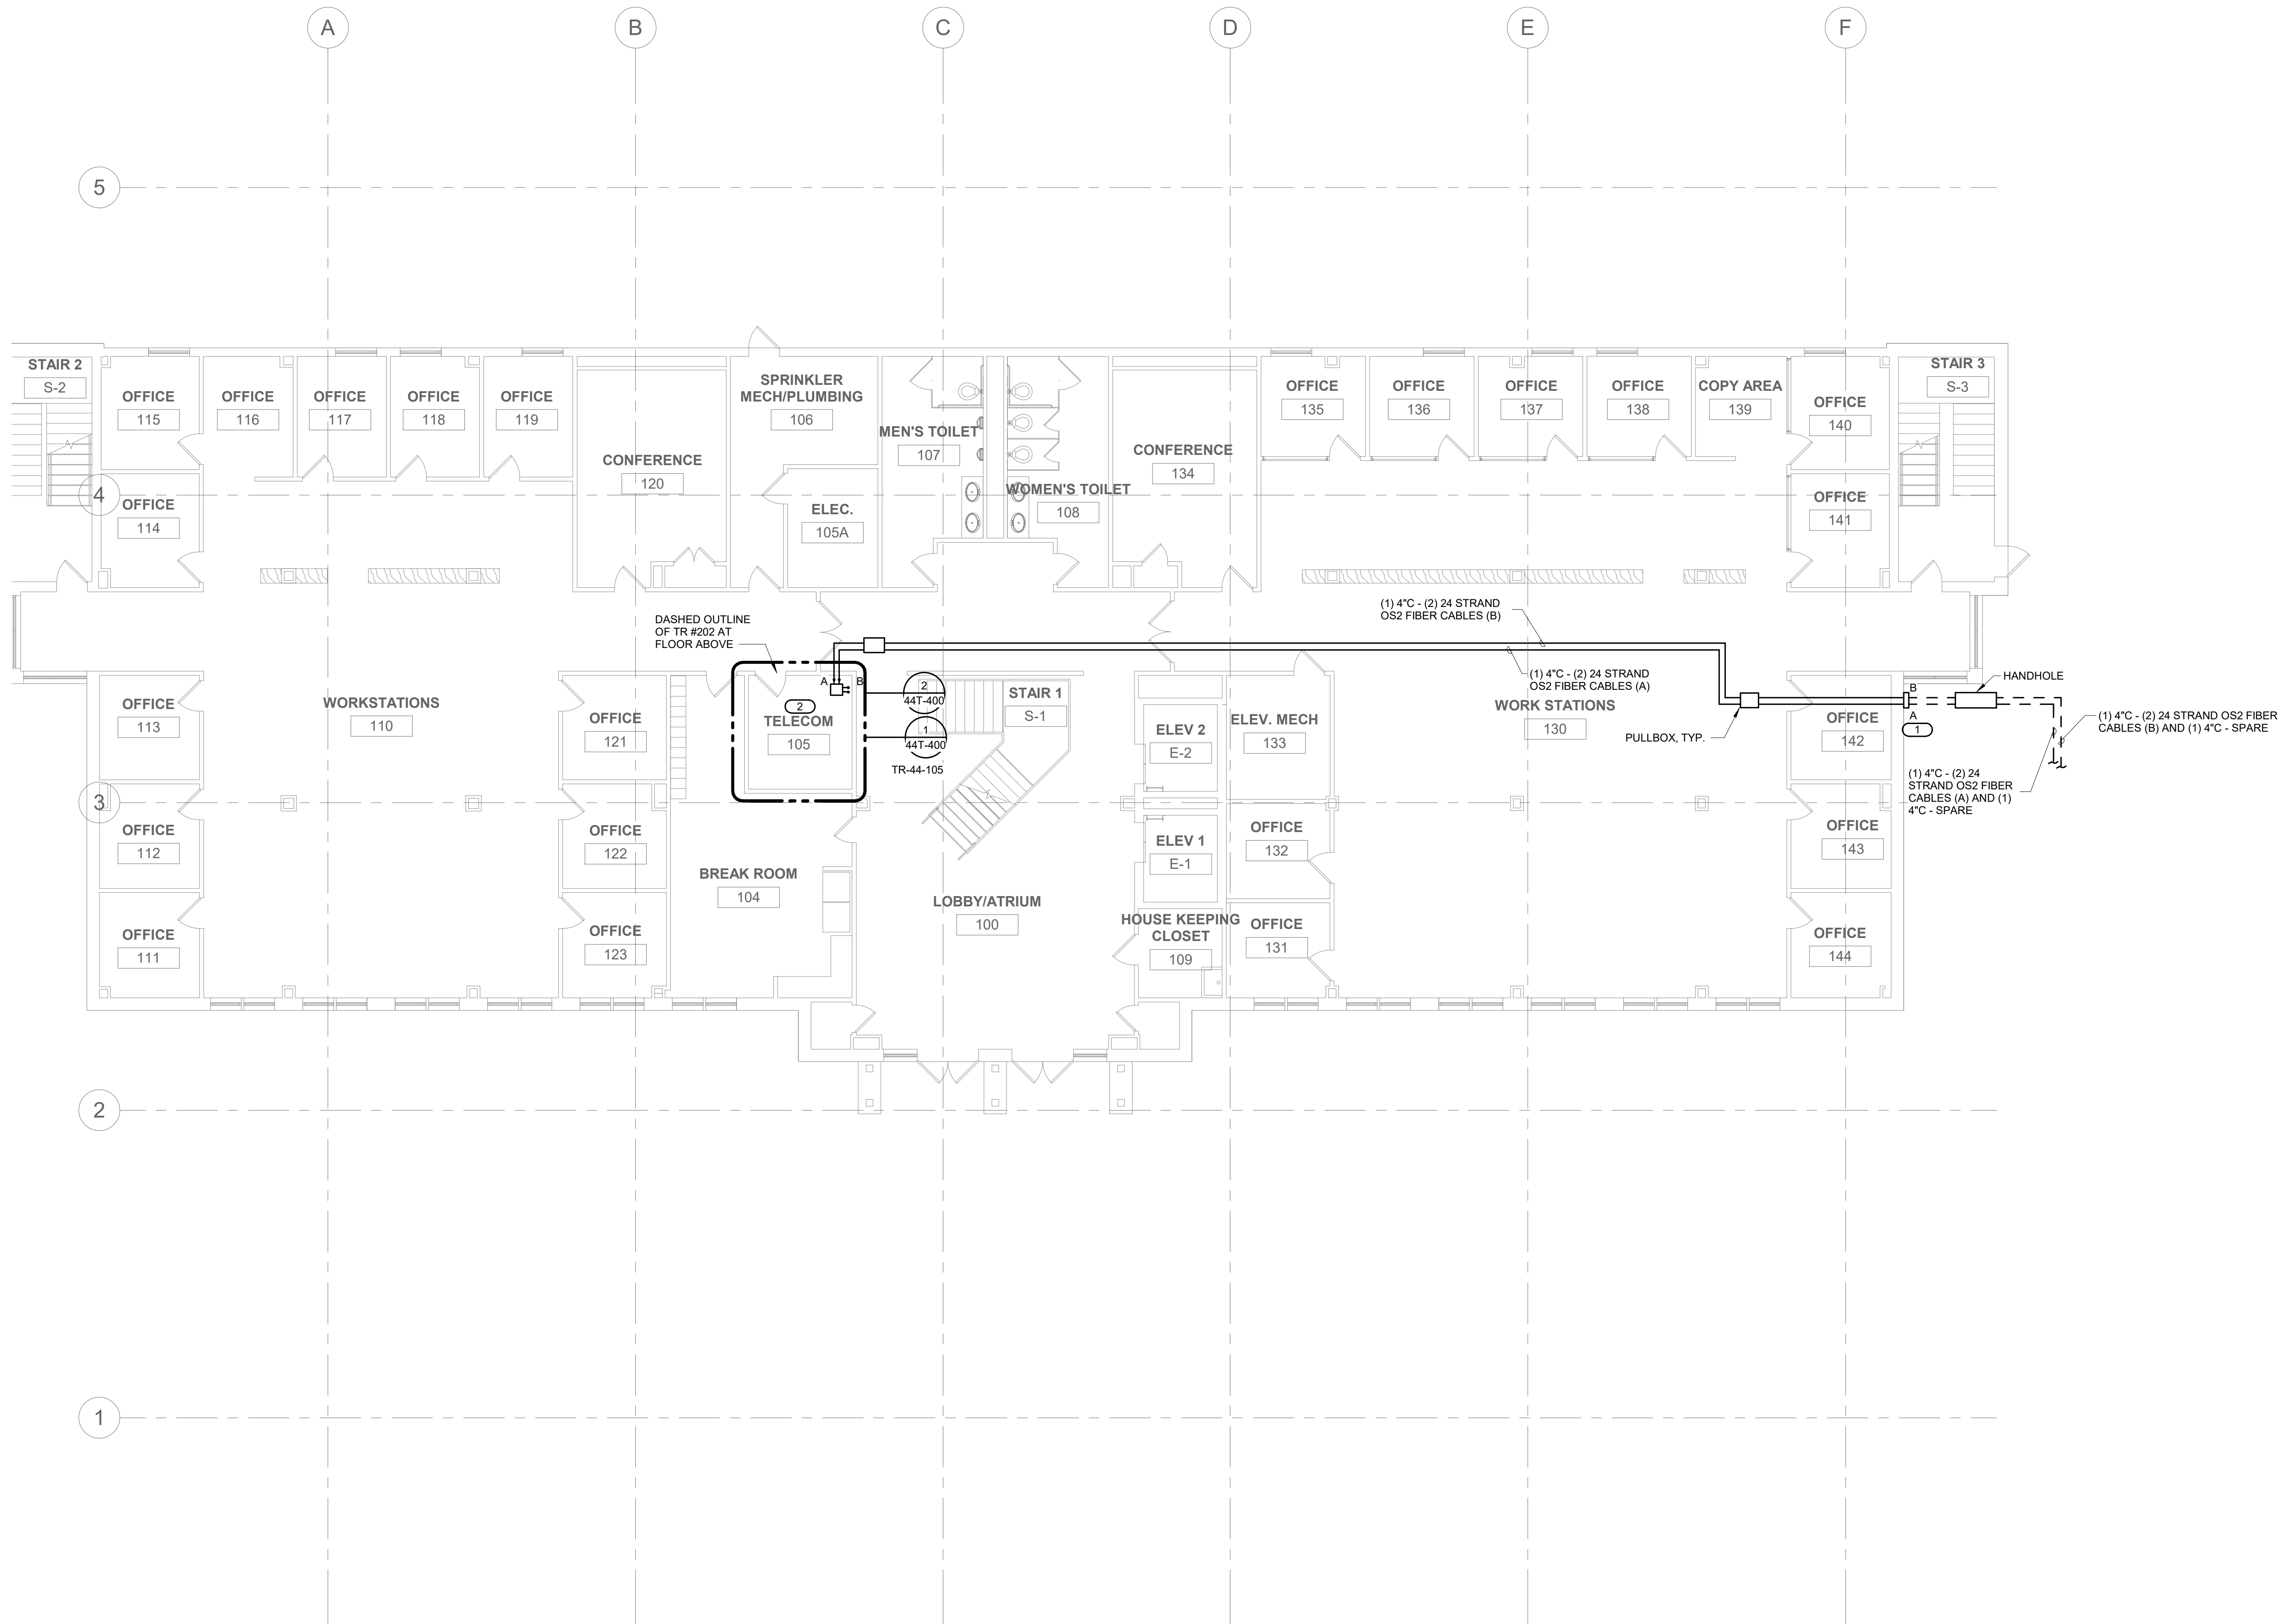

1 LEVEL 01 PLAN - TECHNOLOGY
1/8\"/>

	</
--	--	----

- SHEET NOTES:
1. REFER TO SITEPLAN T5001 FOR ADDITIONAL INFORMATION.


2. REFER TO T500 AND T501 FOR CAMPUS OPTICAL FIBER CABLE RISER DIAGRAMS.

3. REFER TO 217400 FOR HANDHOLE DETAIL.

4. NEW BACKBONE OPTICAL FIBER CABLES SHALL BE INDOOR/OUTDOOR TYPE.

5. ALL BACKBONE OPTICAL FIBER CABLE PATHWAYS SHALL BE NEW. DO NOT RE-USE EXISTING BACKBONE CABLE PATHWAYS FOR NEW BACKBONE CABLES.

6. TRANSITION PVC CONDUITS TO GRC IN CRAWL SPACE OR EXPOSED EXTERIOR LOCATIONS. TRANSITION TO EMT CONDUITS AT INTERIOR OF BUILDING. SEAL ALL PENETRATIONS TO MAINTAIN FIRE-RATINGS OF WALL, CEILING AND FLOORS.
- KEY NOTES: (#)
1. ROUTE CONDUIT UP THRU FLOOR FROM TR #105 AT FLOOR BELOW. CONTINUE ROUTE OF CONDUIT UP TO ABOVE CABLE TRAY.

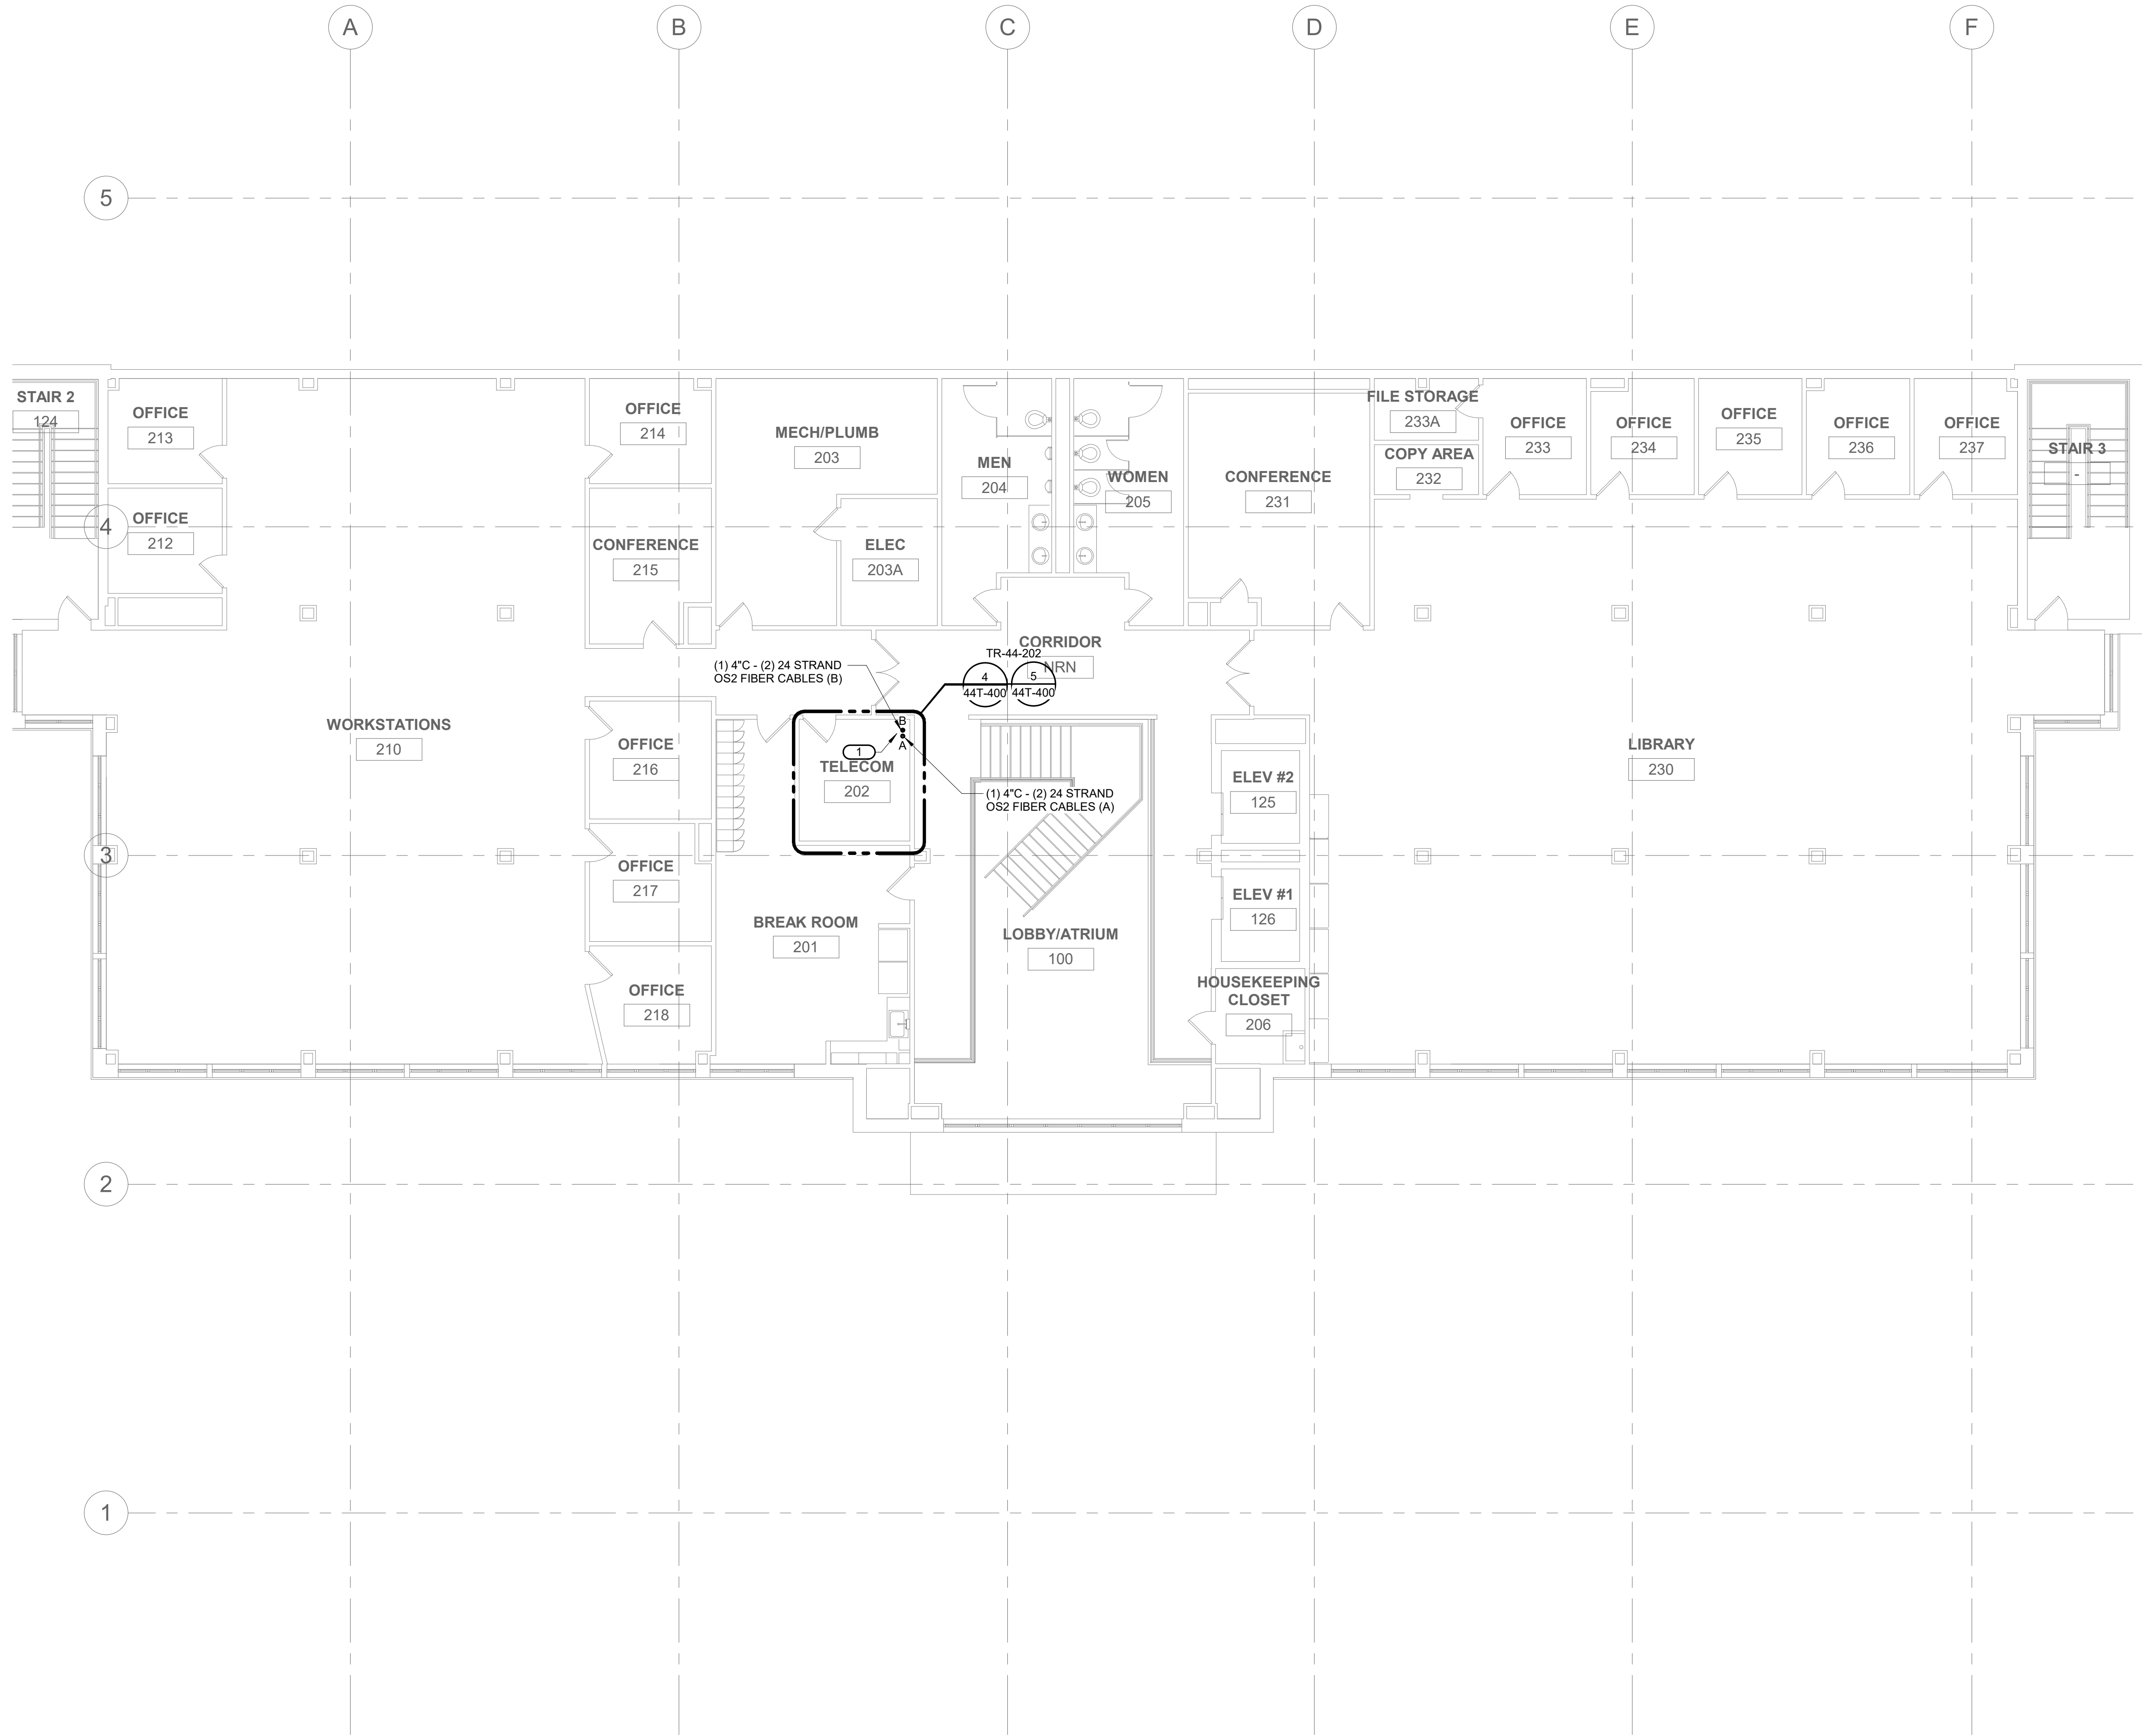

1 LEVEL 02 PLAN - TECHNOLOGY

1/8" = 1'-0"

Revisions:	Date:

CONSULTANT

ENGINEERING DISCIPLINE:



225 W WASHINGTON STREET
SUITE 2700
CHICAGO, IL 60609
P: 312.294.0501 F: 312.294.0003
PROJECT #22010109.00

ARCHITECT/ENGINEER OF RECORD

A/E:

SPEES DESIGN BUILD
23830 PACIFIC HIGHWAY S. SUITE 203
KENT, WA 98032

 SPEESDESIGNBUILD

STAMP



Office of
Construction
and Facilities
Management

 U.S. Department
of Veterans Affairs

Drawing Title
BLDG.44 LEVEL 02 PLAN - TECHNOLOGY
Approved:

Phase
100% CONSTRUCTION DOCUMENTS
FULLY SPRINKLERED

Project Title
EHRM INFRASTRUCTURE UPGRADES - HAMPTON
Location
HAMPTON VA MEDICAL CENTER, HAMPTON, VIRGINIA
Issue Date
05/09/2025
Checked
EW
Drawn
IMEG

Project Number
509-22-700
Building Number
44
Drawing Number
44T-102
661 of 713

BLM 360/509-22-700
VAHampton
E:\H1\509-700\B44.T_R21.rvt
8/20/2025 11:14:58 PM



1

TELECOM ROOM ENLARGEMENT PLAN - TR-44-105

1/2" = 1'-0"

NOTES:

- REFER TO ELECTRICAL DRAWINGS FOR ROOM LAYOUT AND RACK ELEVATIONS.
- ROUTE OPTICAL FIBER CABLES TO OVERHEAD CABLE TRAYS AND TERMINATE IN FIBER DISTRIBUTION CABINET

KEYNOTES: (P)

- THROUGH WALL PENETRATION FOR BACKBONE CONDUIT. OPTICAL FIBER CABLES CONTINUE ON CABLE TRAY TO RACKS.



2

TELECOM ROOM PATHWAYS - TR-44-105

1/2" = 1'-0"



4

TELECOM ROOM ENLARGEMENT PLAN - TR-44-202

1/2" = 1'-0"

NOTES:

- REFER TO ELECTRICAL DRAWINGS FOR ROOM LAYOUT AND RACK ELEVATIONS.
- ROUTE OPTICAL FIBER CABLES TO OVERHEAD CABLE TRAYS AND TERMINATE IN FIBER DISTRIBUTION CABINET

KEYNOTES: (P)

- THROUGH FLOOR/CEILING PENETRATION FOR BACKBONE CONDUIT. CONTINUE CONDUIT UP TO ABOVE CABLE TRAY. OPTICAL FIBER CABLES CONTINUE ON CABLE TRAY TO RACKS.




5

TELECOM ROOM PATHWAYS - TR-44-202


1/2" = 1'-0"

LEVEL 02

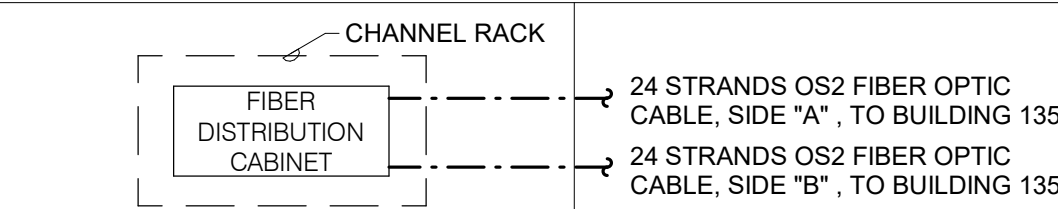

TELECOMMUNICATIONS ROOM TR-44-202

LEVEL 01

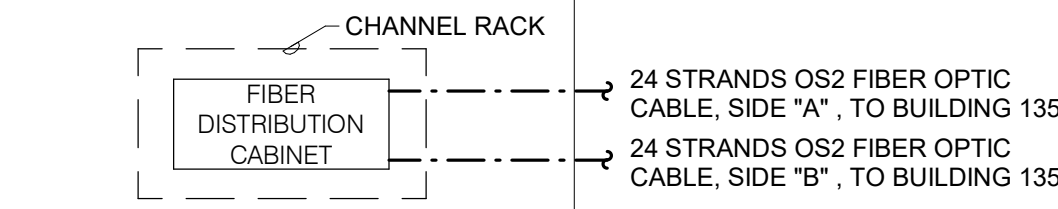

TELECOMMUNICATIONS ROOM TR-44-105

3

FIBER RISER DIAGRAM

NO SCALE

NOTES:

- THIS RISER IS DIAGMMATIC AND MAY NOT SHOW ACTUAL ROUTING OR QUANTITIES OF MATERIALS SHOWN. THIS RISER IS SHOWN FOR CLARIFICATION OF CONNECTION(S), LOCATIONS AND CABLE TYPE. ALL INFORMATION OUTLETS ARE TYPICAL OF THE OUTLETS IN THE AREA SHOWN. REFER TO FLOOR PLANS FOR MORE SPECIFIC ROUTING INFORMATION. REFER TO SPECIFICATIONS FOR ADDITIONAL REQUIREMENTS.
- REFER TO ELECTRICAL DRAWINGS FOR CHANNEL RACK AND FIBER OPTIC DISTRIBUTION CABINET SPECIFICATIONS

Revisions:	Date:

CONSULTANT

ENGINEERING DISCIPLINE:



225 W WASHINGTON STREET
SUITE 2700
CHICAGO, IL 60606
P: 312.294.0501 F: 312.294.0003
PROJECT #22010109.00

ARCHITECT/ENGINEER OF RECORD

A/E:

SPEES DESIGN BUILD
23830 PACIFIC HIGHWAY S. SUITE 203
KENT, WA 98032



STAMP



Office of
Construction
and Facilities
Management



U.S. Department
of Veterans Affairs

Drawing Title
BLDG.44 TECHNOLOGY ENLARGED PLANS

Approved:

Phase
100% CONSTRUCTION
DOCUMENTS

FULLY SPRINKLERED

Project Title
EHRM INFRASTRUCTURE
UPGRADES - HAMPTON

Location
HAMPTON VA MEDICAL CENTER, HAMPTON, VIRGINIA

Issue Date
05/09/2025

Checked
EW

Drawn
IMEG

Project Number
509-22-700

Building Number
44

Drawing Number
44T-400

662 of 713

- SHEET NOTES:
1. REFER TO SITEPLAN TS001 FOR ADDITIONAL INFORMATION.

2. REFER TO TS00 AND TS01 FOR CAMPUS OPTICAL FIBER CABLE RISER DIAGRAMS.


3. REFER TO 2/T400 FOR HANDHOLE DETAIL.

4. NEW BACKBONE OPTICAL FIBER CABLES SHALL BE INDOOR/OUTDOOR TYPE.

5. ALL BACKBONE OPTICAL FIBER CABLE PATHWAYS SHALL BE NEW. DO NOT RE-USE EXISTING BACKBONE CABLE PATHWAYS FOR NEW BACKBONE CABLES.

6. TRANSITION PVC CONDUITS TO GRC IN CRAWL SPACE OR EXPOSED EXTERIOR LOCATIONS. TRANSITION TO EMT CONDUITS AT INTERIOR OF BUILDING.
- KEY NOTES: C #
1. PROVIDE PULLBOX ON EXTERIOR WALL AT HEIGHT OF CRAWL SPACE CEILING. PROVIDE PENETRATION THRU WALL. ROUTE CONDUIT UP THRU PULLBOX AND THRU WALL INTO CRAWL SPACE.

2. CONTINUE TO ROUTE IN CRAWL SPACE TO LOCATION BELOW. CLOSET IN FOYER. PROVIDE PENETRATION THRU CRAWL SPACE AND FIRST FLOOR CEILING AND ROUTE CONDUITS UP TO ABOVE HEIGHT OF TE #110.

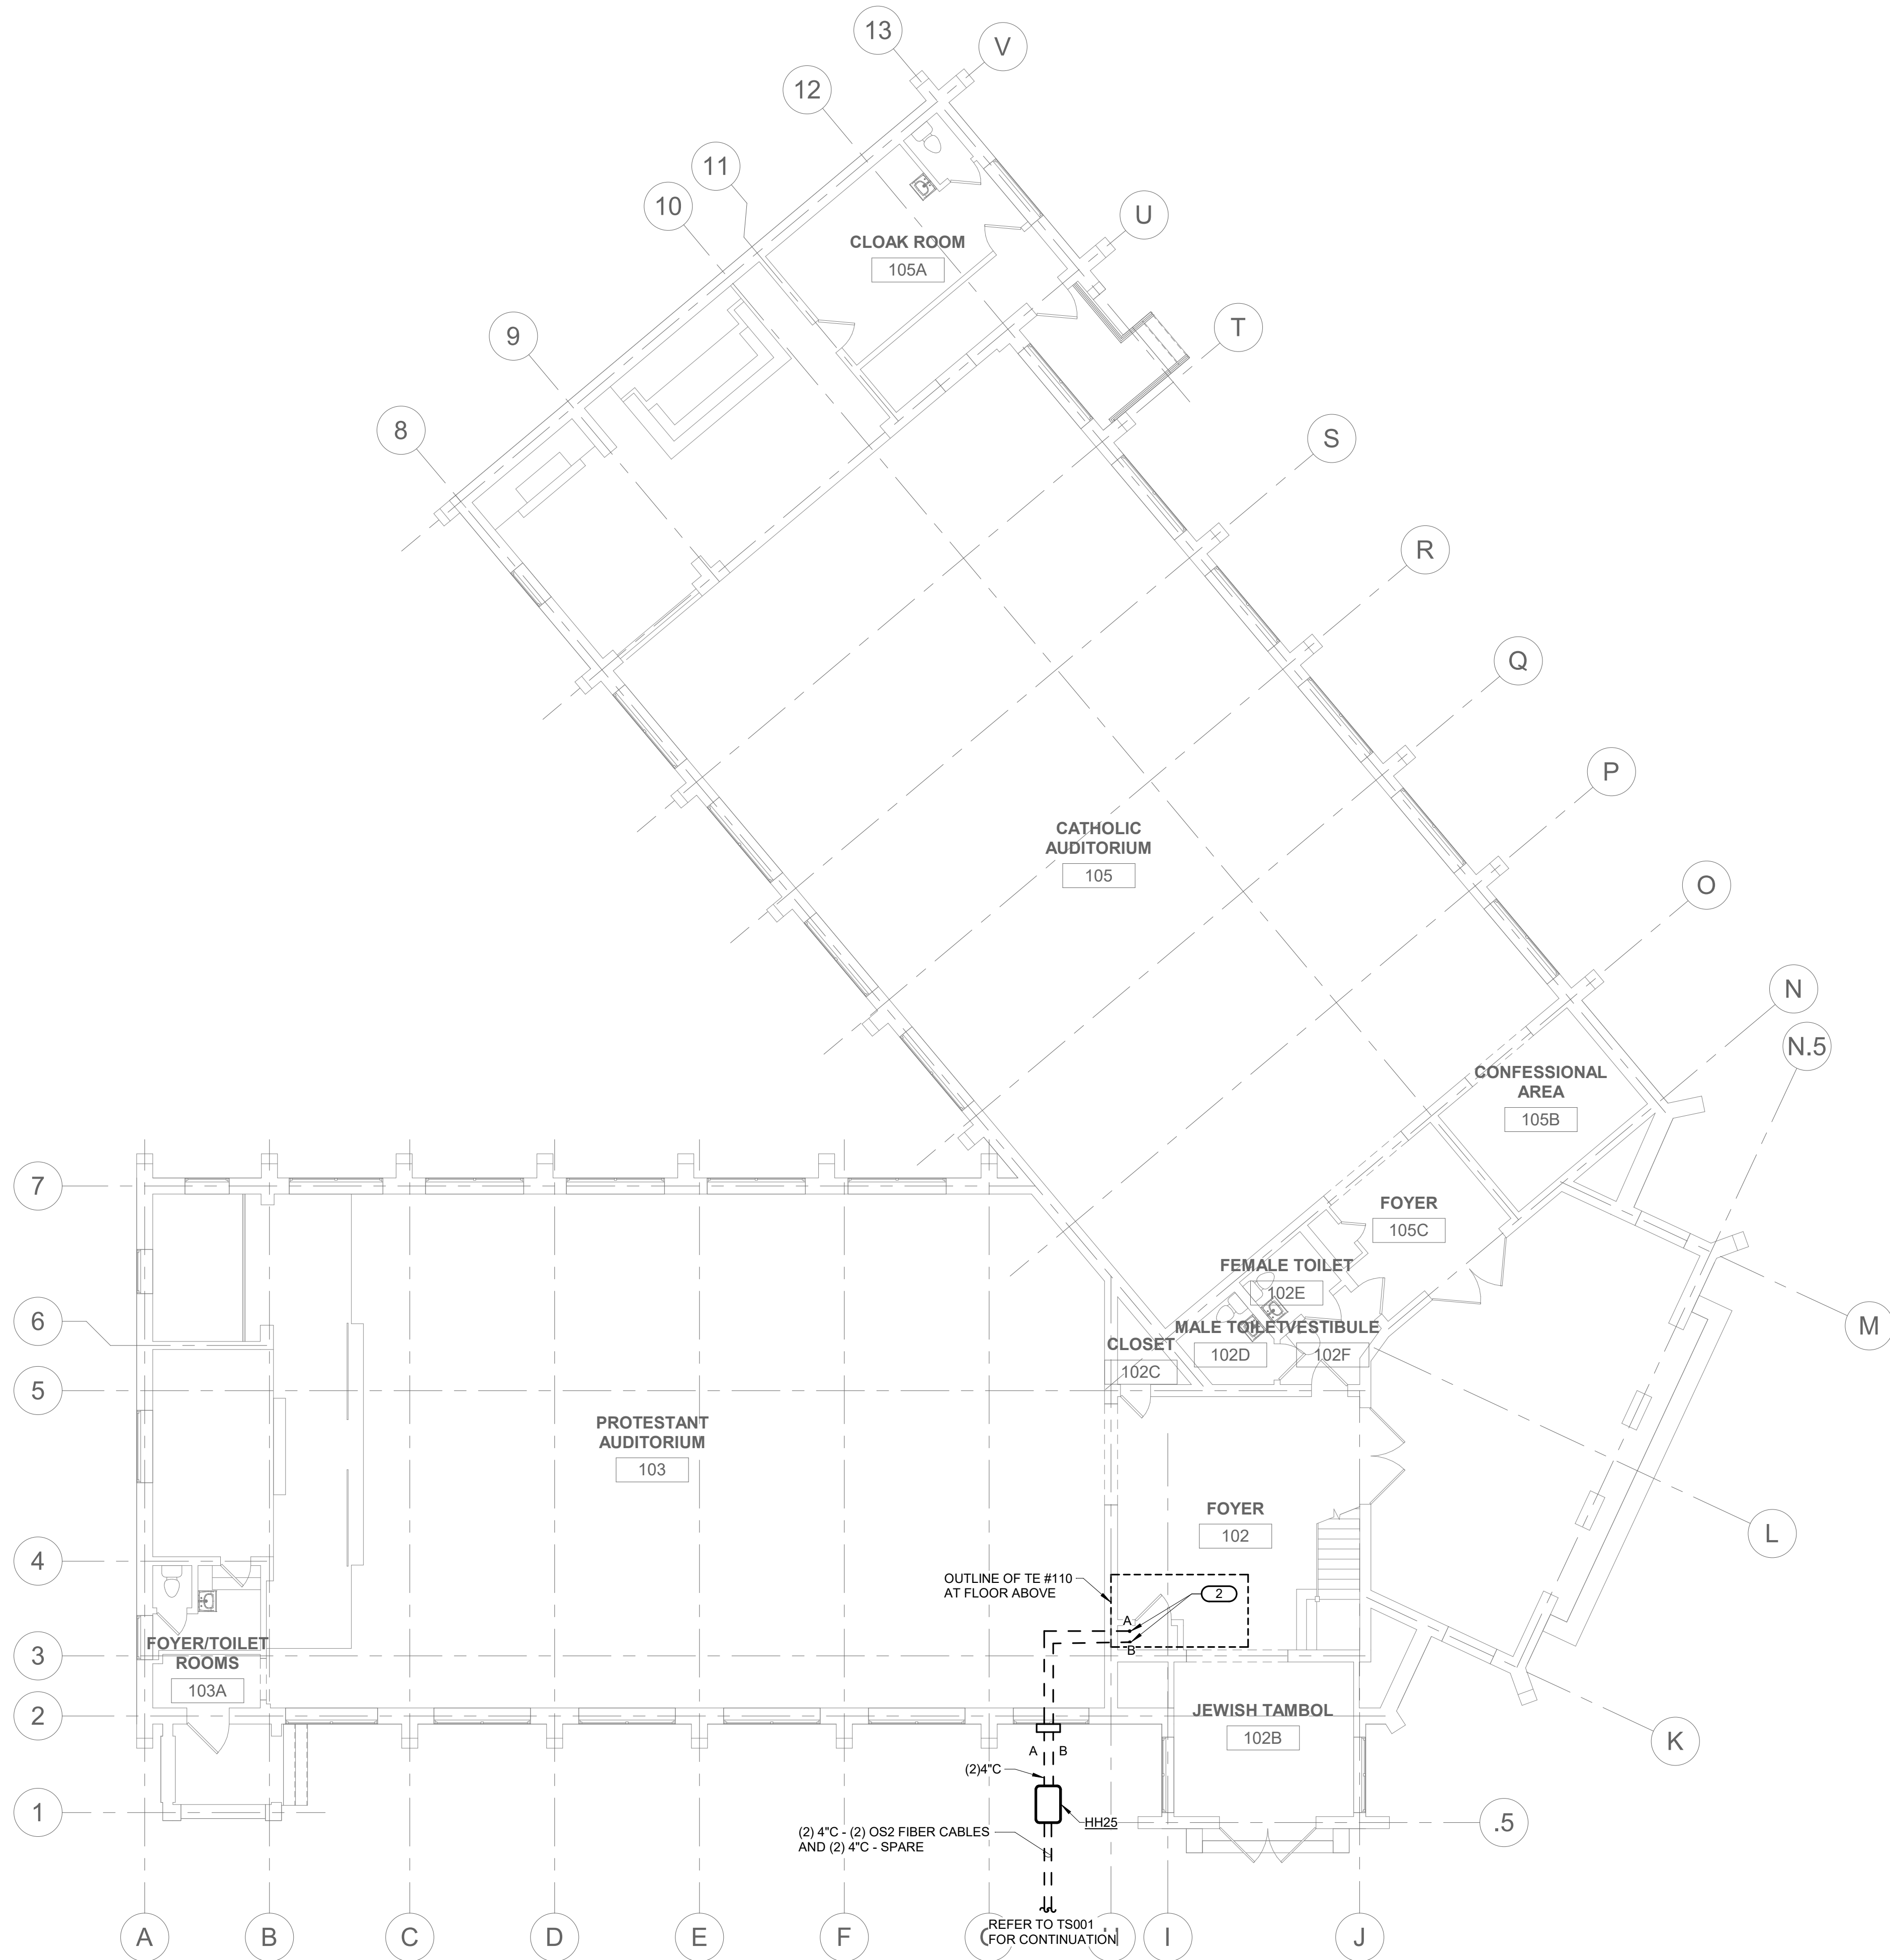

 **1** **LEVEL 01 PLAN - TECHNOLOGY**
1/8" = 1'-0"

--	--	

BLM 360/509-22-700
VAHampton
E:\H135-700\B46.T_R21.rvt

8/13/2025 1:29:41 PM

VA FORM 08 - 6231

Revisions:	Date:

CONSULTANT

ENGINEERING DISCIPLINE:


www.imegcorp.com
225 W WASHINGTON STREET
SUITE 2700
CHICAGO, IL 60606
P: 312.294.0501 F: 312.294.0003
PROJECT #22010109.00

ARCHITECT/ENGINEER OF RECORD

A/E:

SPEES DESIGN BUILD
23830 PACIFIC HIGHWAY S. SUITE 203
KENT, WA 98032

 SPEESDESIGNBUILD

STAMP



Office of
Construction
and Facilities
Management

 U.S. Department
of Veterans Affairs

Drawing Title

BLDG.48 TECHNOLOGY DETAILS AND
DIAGRAMS

Approved:

Phase

100% CONSTRUCTION
DOCUMENTS

FULLY SPRINKLERED

Project Title

EHRM INFRASTRUCTURE
UPGRADES - HAMPTON

Location

HAMPTON VA MEDICAL CENTER, HAMPTON, VIRGINIA

Issue Date

05/09/2025

Checked

EW

Drawn

IMEG

Project Number

509-22-700

Building Number

48

Drawing Number

48T-400

665 of 713



--	--	

[illegible]

BIM 360://509-22-700
VAHampton
EHRM/509-700.B66.T_R21.rvt

B:\A\360\509-22-700
VAHampton
E:\A\360-700-666.T_R21.rvt
8/13/2025 1:32:34 PM

VA FORM 08 - 6231

CONSULTANT
ENGINEERING DISCIPLINE:
IMEG
www.imegcorp.com
225 W WASHINGTON STREET
SUITE 2700
CHICAGO, IL 60606
P: 312.294.0501 F: 312.294.0003
PROJECT #22010109.00

ARCHITECT/ENGINEER OF RECORD
A/E:
SPEES DESIGN BUILD
23830 PACIFIC HIGHWAY S. SUITE 203
KENT, WA 98032
SDB SPEESDESIGNBUILD

STAMP
REGISTERED COMMUNICATIONS DISTRIBUTION DESIGNER
Bicsi
ES&C WIRE-2
Reg. No. 1979026
EXPIRES 03-01-2025
RCDD
John P. Bicsi

Office of
Construction
and Facilities
Management
VA U.S. Department
of Veterans Affairs


Drawing Title
BLDG.66 TECHNOLOGY DETAILS AND
DIAGRAMS
Approved:

Phase
100% CONSTRUCTION
DOCUMENTS
FULLY SPRINKLERED

Project Title
EHRM INFRASTRUCTURE
UPGRADES - HAMPTON
Location
HAMPTON VA MEDICAL CENTER, HAMPTON, VIRGINIA
Issue Date
05/09/2025
Checked
EW
Drawn
IMEG

Project Number
509-22-700
Building Number
66
Drawing Number
66T-400
668 of 713

- SHEET NOTES:**
 - REFER TO SITEPLAN TS001 FOR ADDITIONAL INFORMATION.
 - REFER TO TS00 AND TS01 FOR CAMPUS OPTICAL FIBER CABLE RISER DIAGRAMS.
 - REFER TO 27T400 FOR HANDHOLE DETAIL.
 - NEW BACKBONE OPTICAL FIBER CABLES SHALL BE INDOOR/OUTDOOR TYPE.
 - ALL BACKBONE OPTICAL FIBER CABLE PATHWAYS SHALL BE NEW. DO NOT RE-USE EXISTING BACKBONE CABLE PATHWAYS FOR NEW BACKBONE CABLES.
 - TRANSITION PVC CONDUITS TO GRC IN CRAWL SPACE OR EXPOSED EXTERIOR LOCATIONS. TRANSITION TO EMT CONDUITS AT INTERIOR OF BUILDING. SEAL ALL PENETRATIONS TO MAINTAIN FIRE-RATINGS OF WALL, CEILING AND FLOORS.
- KEY NOTES:** **C** #
 - PROVIDE PULLBOX ON EXTERIOR WALL AT HEIGHT ABOVE FINISHED CEILING. ROUTE CONDUIT UP WALL INTO PULLBOX. PROVIDE PENETRATION THRU WALL AND ROUTE CONDUIT ABOVE CEILING THRU CORRIDORS INTO TR #102.

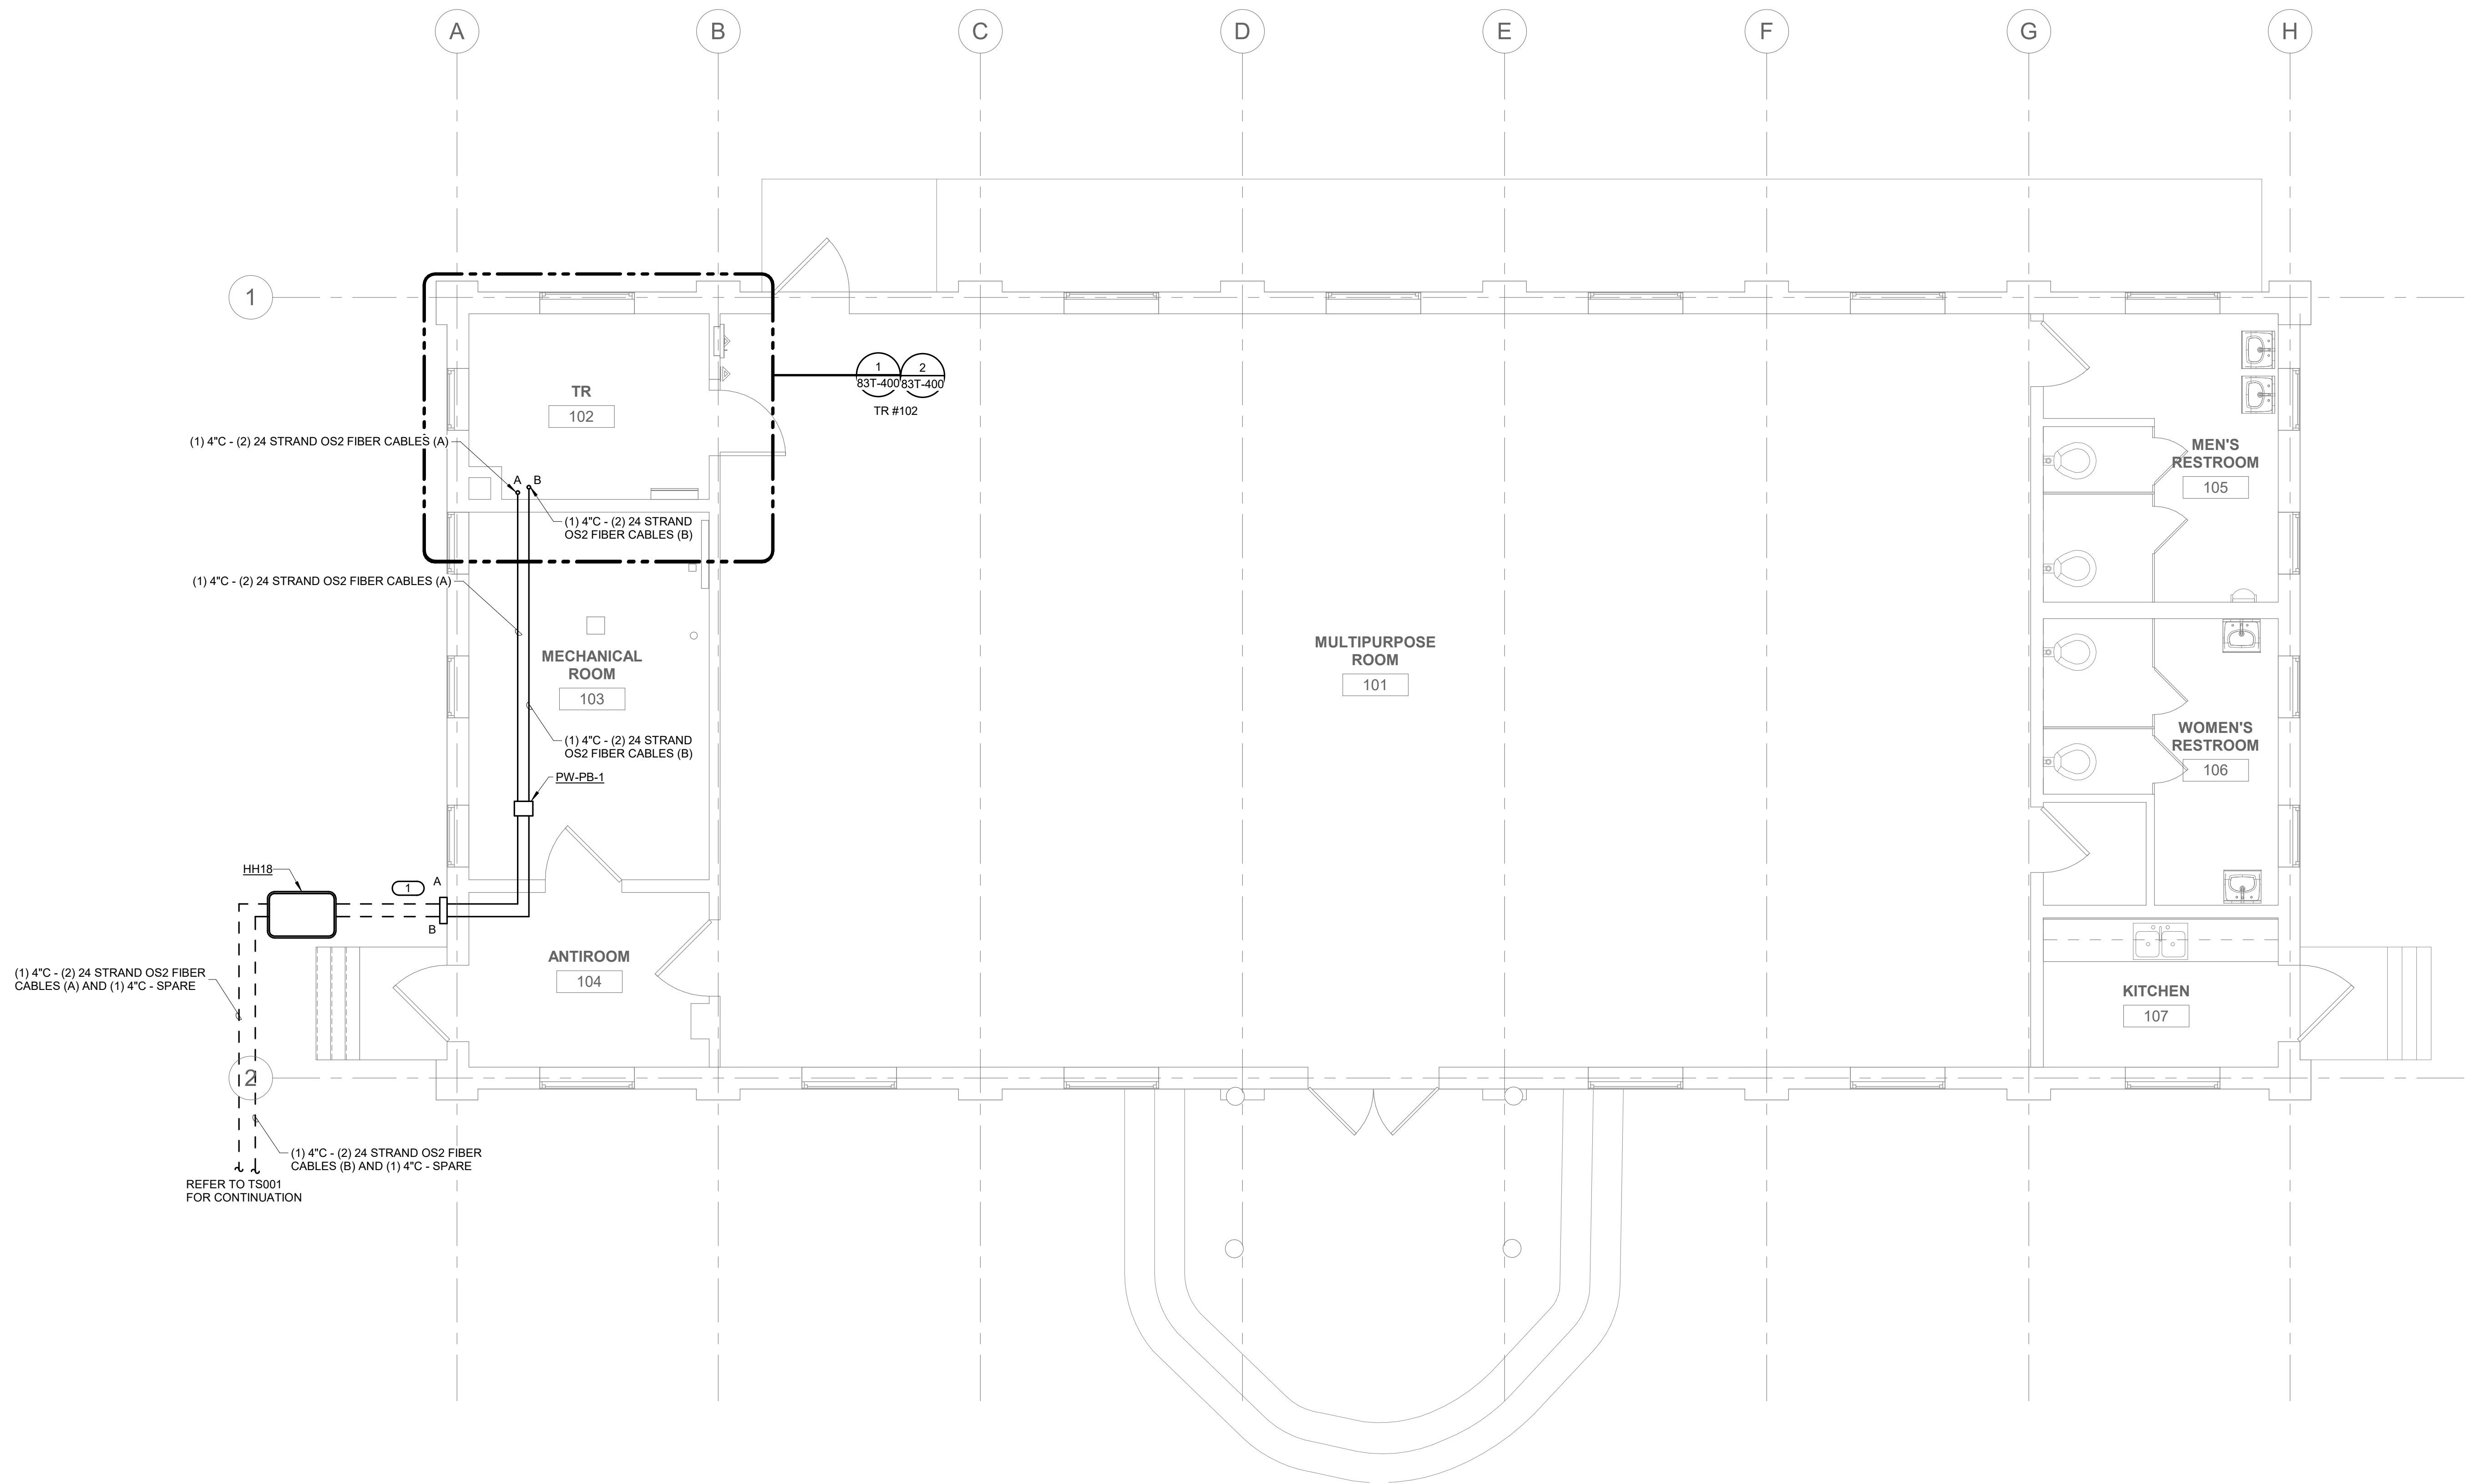


1 LEVEL 01 PLAN - TECHNOLOGY
1/4" = 1'-0"

B:\M_360\509-22-700
VAHampton
EHRM\509-22-700.B65.T_021.rvt

8/13/2025 1:41:30 PM

VA FORM 08 - 6231

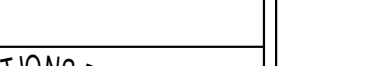		CONSULTANT	ARCHITECT/ENGINEER OF RECORD	STAMP	Office of Construction and Facilities Management	Drawing Title	Phase	Project Title	Project Number		
		ENGINEERING DISCIPLINE:	A/E:			BLDG.83 LEVEL 01 PLAN - TECHNOLOGY	100% CONSTRUCTION DOCUMENTS	EHRM INFRASTRUCTURE UPGRADES - HAMPTON	509-22-700		
			SPEES DESIGN BUILD 23830 PACIFIC HIGHWAY S. SUITE 203 KENT, WA 98032					Building Number			
		www.imegcorp.com					83	Drawing Number			
		225 W WASHINGTON STREET SUITE 2700 CHICAGO, IL 60606 P: 312.294.0501 F: 312.294.0003 PROJECT #22010109.00	 SPEESDESIGNBUILD					83T-201			
Revisions:	Date:			RCDD	VA U.S. Department of Veterans Affairs	Approved:	FULLY SPRINKLERED	Location HAMPTON VA MEDICAL CENTER, HAMPTON, VIRGINIA	669 of 713		
								Issue Date 05/09/2025	Checked EW	Drawn IMEG	

BM 360/509-22-700
VAHampton
E:\M\509-22-700\BES.T_R21.rvt

8/13/2025 1:41:31 PM

VA FORM 08 - 6231

Revisions:	Date:

CONSULTANT
ENGINEERING DISCIPLINE:

225 W WASHINGTON STREET SUITE 2700 CHICAGO, IL 60606 P: 312.294.0501 F: 312.294.0003 PROJECT #22010109.00

ARCHITECT/ENGINEER OF RECORD
A/E:
SPEES DESIGN BUILD 23830 PACIFIC HIGHWAY S. SUITE 203 KENT, WA 98032
 SPEESDESIGNBUILD

STAMP



Office of Construction and Facilities Management
 U.S. Department of Veterans Affairs

Drawing Title
BLDG.83 TECHNOLOGY DETAILS AND DIAGRAMS
Approved:

Phase
100% CONSTRUCTION DOCUMENTS
FULLY SPRINKLERED

Project Title
EHRM INFRASTRUCTURE UPGRADES - HAMPTON
Location
HAMPTON VA MEDICAL CENTER, HAMPTON, VIRGINIA
Issue Date
05/09/2025
Checked
EW
Drawn
IMEG

Project Number
509-22-700
Building Number
83
Drawing Number
83T-400
670 of 713

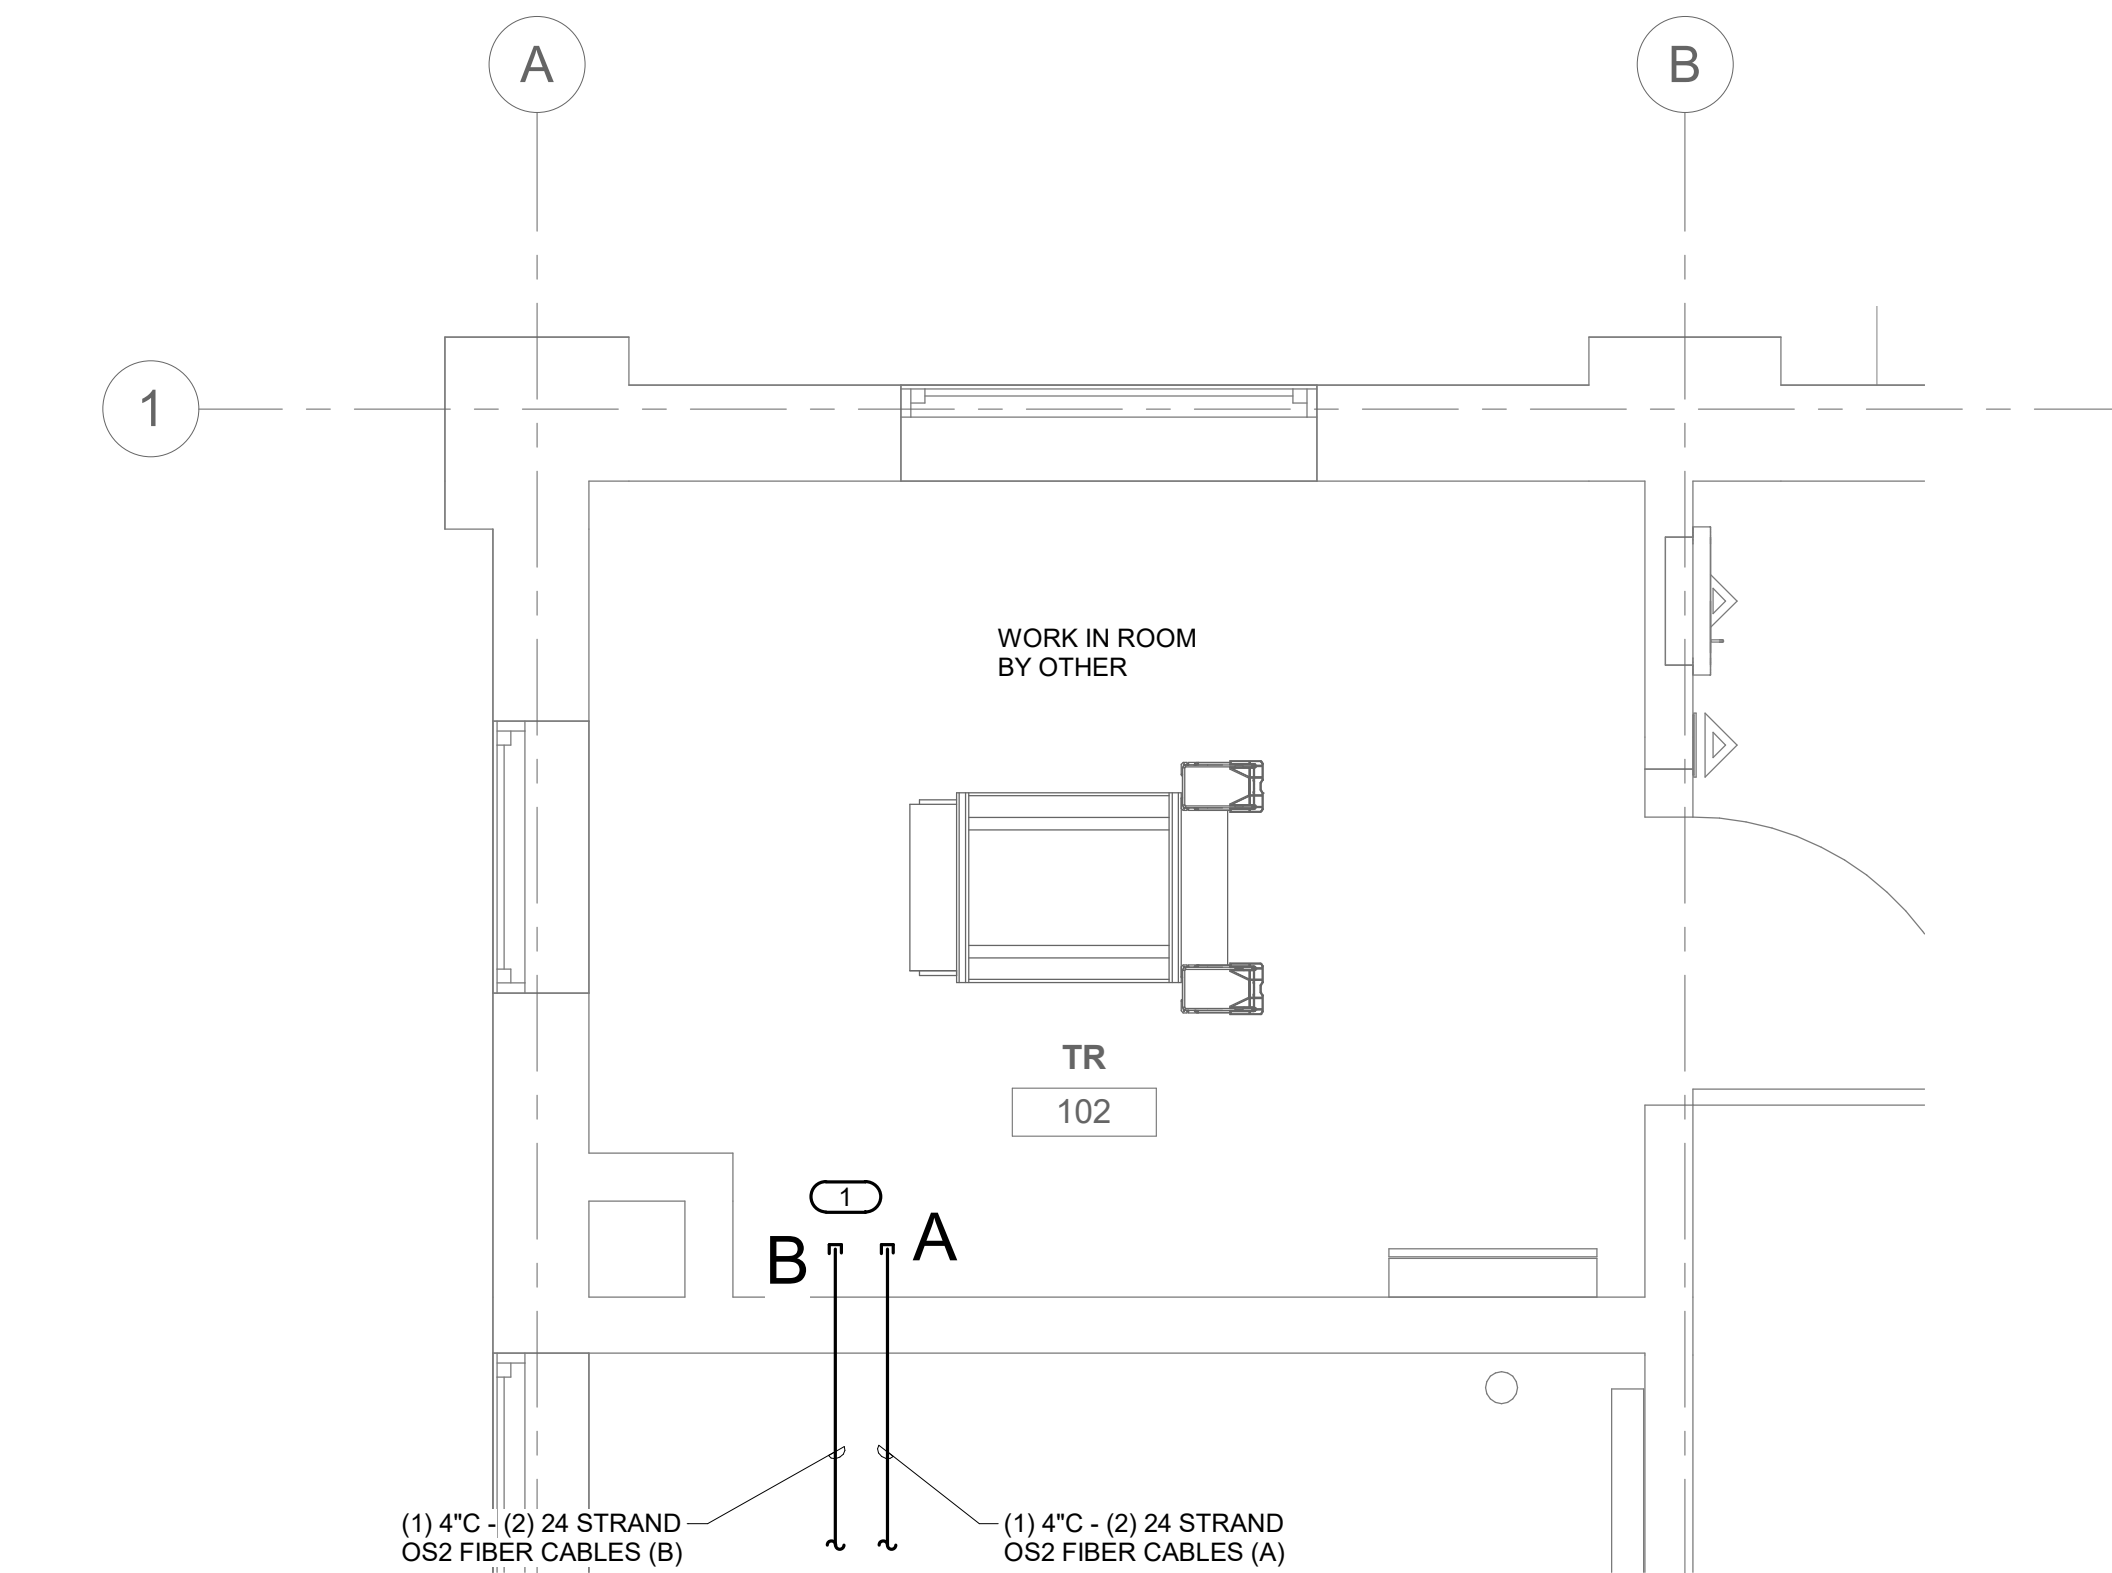

1 TELECOM ROOM ENLARGEMENT TR #102


1/2" = 1'-0"

NOTES:

1. REFER TO ELECTRICAL DRAWINGS FOR ROOM LAYOUT AND RACK ELEVATIONS.
2. ROUTE OPTICAL FIBER CABLE TO OVERHEAD CABLE TRAY AND TERMINATE IN FIBER DISTRIBUTION CABINET.


KEY NOTES:

1. THROUGH WALL PENETRATION FOR BACKBONE CONDUIT. OPTICAL FIBER CABLE CONTINUES ON CABLE TRAY TO RACKS.

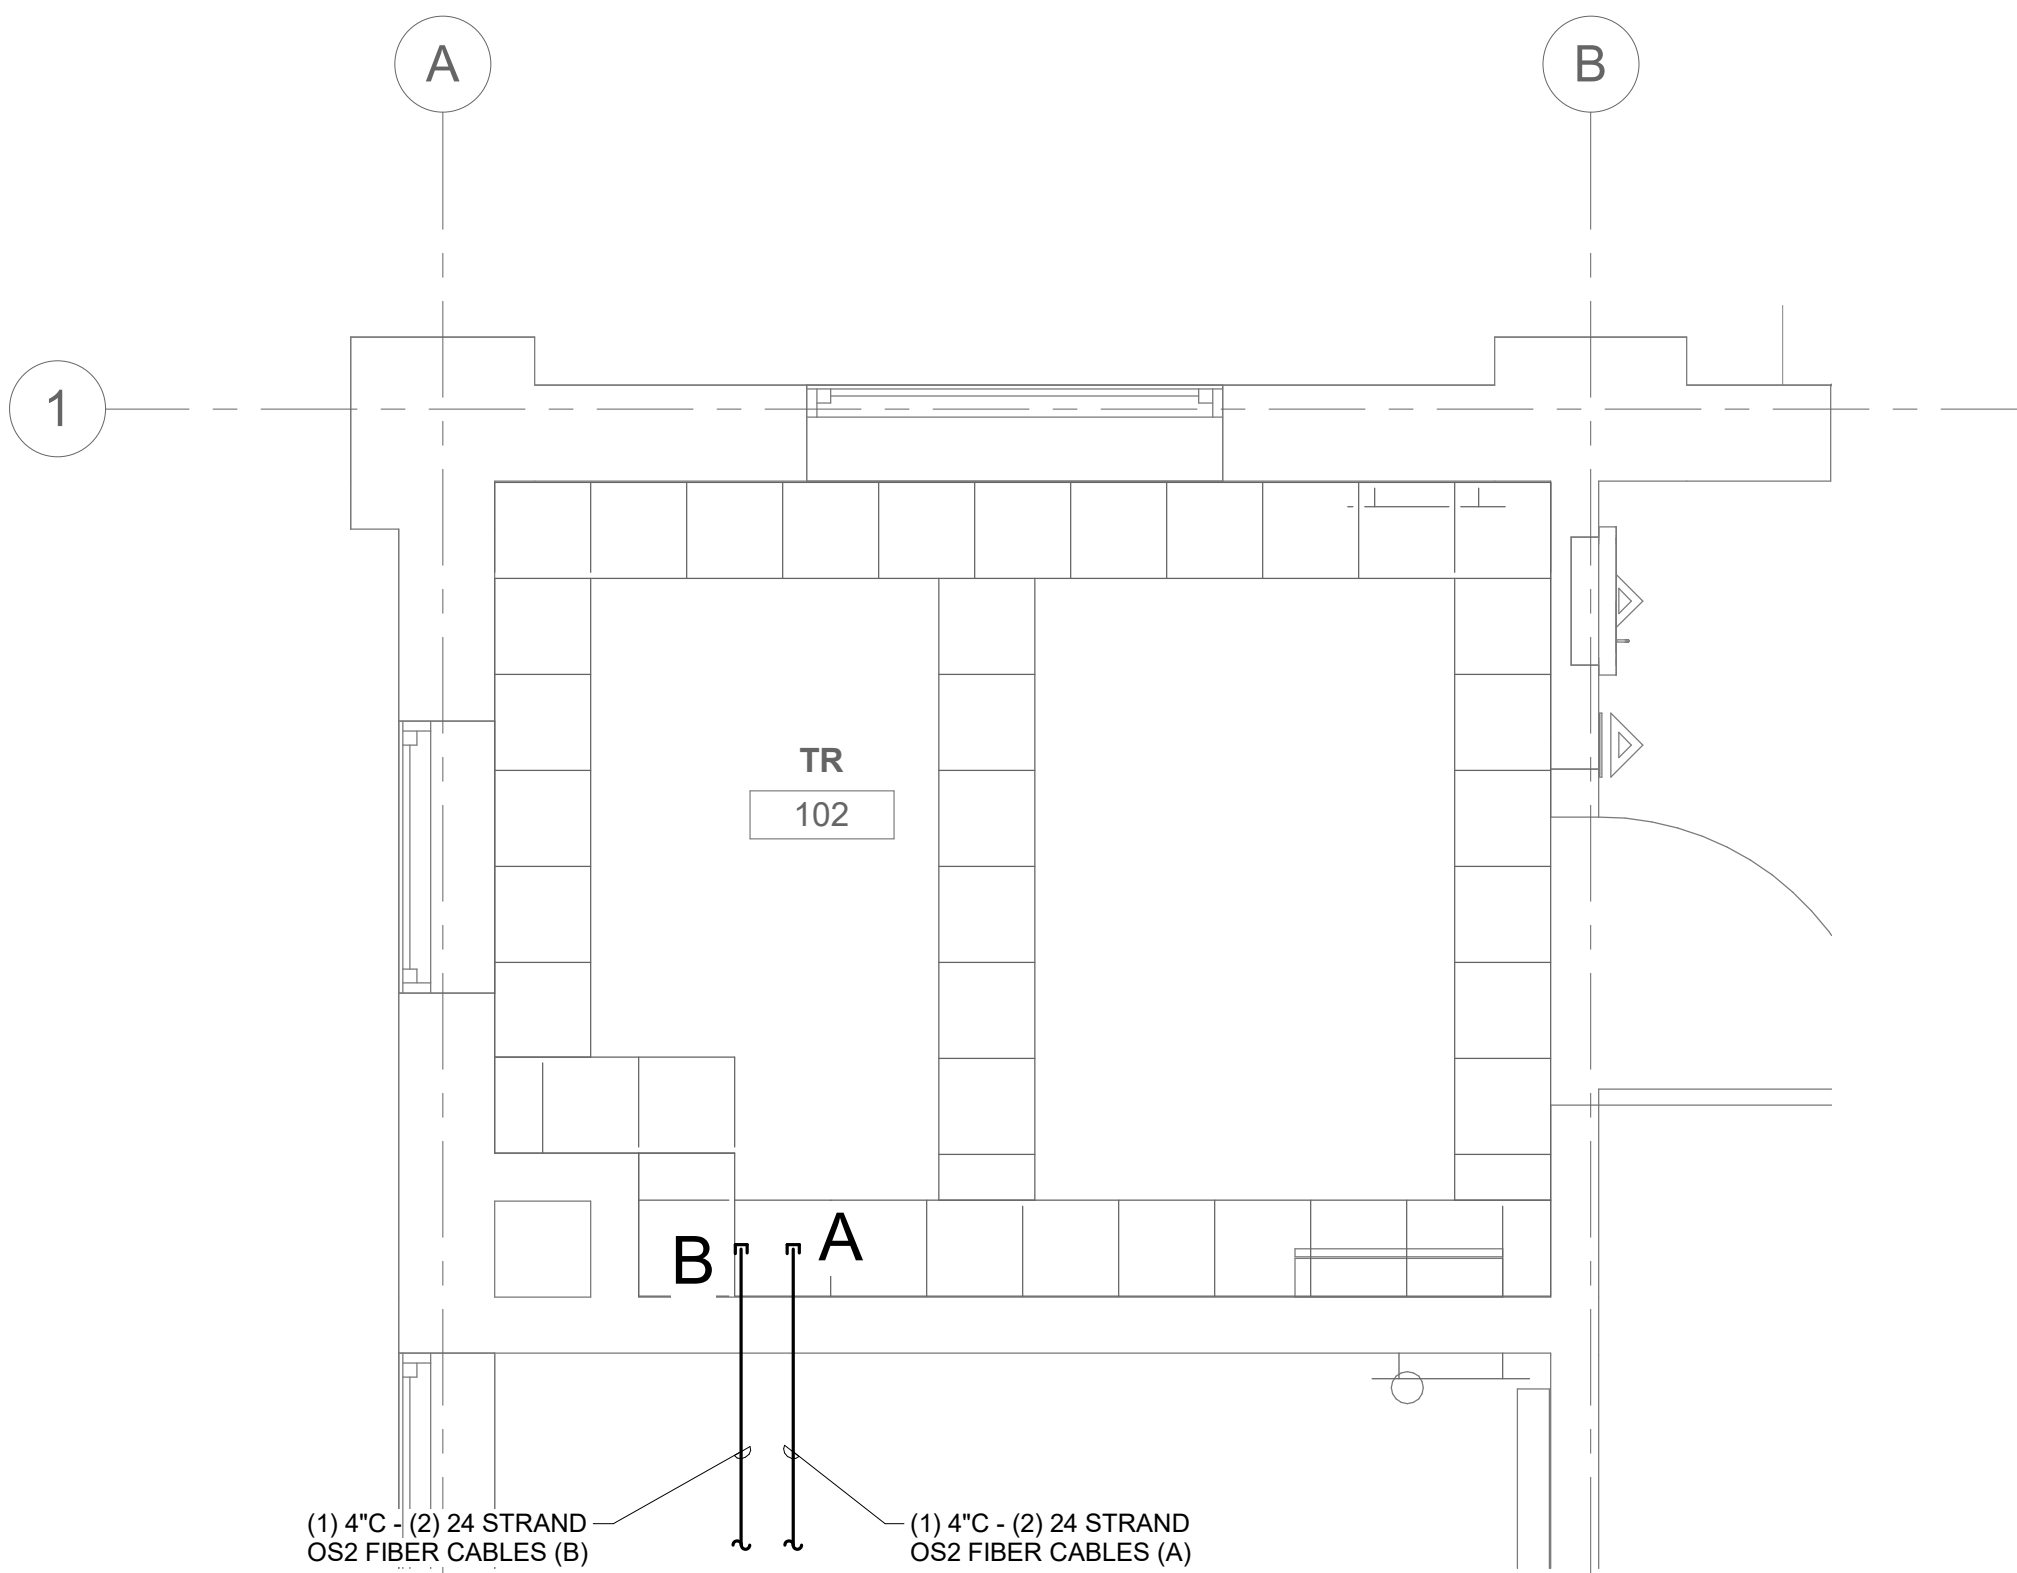

2 TELECOM ROOM PATHWAY TR #102

1/2" = 1'-0"

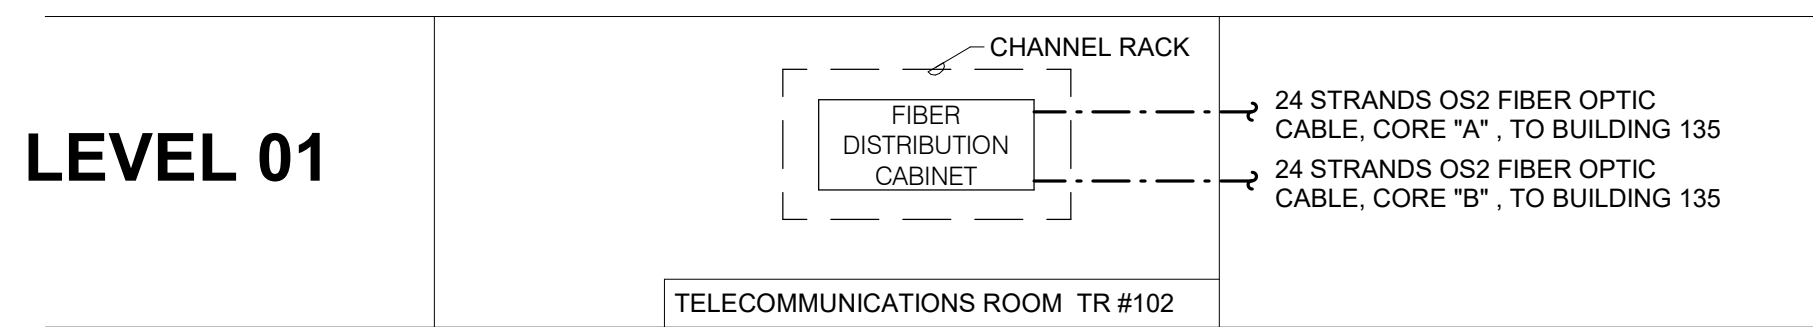

3 FIBER RISER DIAGRAM


NO SCALE

NOTES:

1. THIS RISER IS DIAGRAMMATIC AND MAY NOT SHOW ACTUAL ROUTING OR QUANTITIES OF MATERIALS SHOWN. THIS RISER IS SHOWN FOR CLARIFICATION OF CONNECTION(S), LOCATIONS AND CABLE TYPE. ALL INFORMATION OUTLETS ARE TYPICAL OF THE OUTLETS IN THE AREA SHOWN. REFER TO FLOOR PLANS FOR MORE SPECIFIC ROUTING INFORMATION. REFER TO SPECIFICATIONS FOR ADDITIONAL REQUIREMENTS.
2. REFER TO ELECTRICAL DRAWINGS FOR CHANNEL RACK AND FIBER OPTIC DISTRIBUTION CABINET SPECIFICATIONS

A
B
C
D
E
F

- SHEET NOTES:**
 1. REFER TO SITEPLAN TS001 FOR ADDITIONAL INFORMATION.
 2. REFER TO TS00 AND TS01 FOR CAMPUS OPTICAL FIBER RISER DIAGRAMS.
 3. REFER TO 2/1400 FOR HANDHOLE DETAIL.
 4. REFER TO ENLARGED PLANS FOR ADDITIONAL INFORMATION.
 5. ROUTES SHOWN THRU CRAWL SPACE ARE "SUGGESTED" ROUTES. FIELD VERIFY EXACT ROUTES IN CRAWL SPACE.
 6. SEAL ALL PENETRATIONS TO MAINTAIN FIRE-RATINGS OF WALL, CEILING AND FLOORS.
- KEY NOTES:** (#)
 1. ROUTE CONDUITS ABOVE CORRIDOR CEILINGS TO TR # 2A-154A IN BLDG 110B.

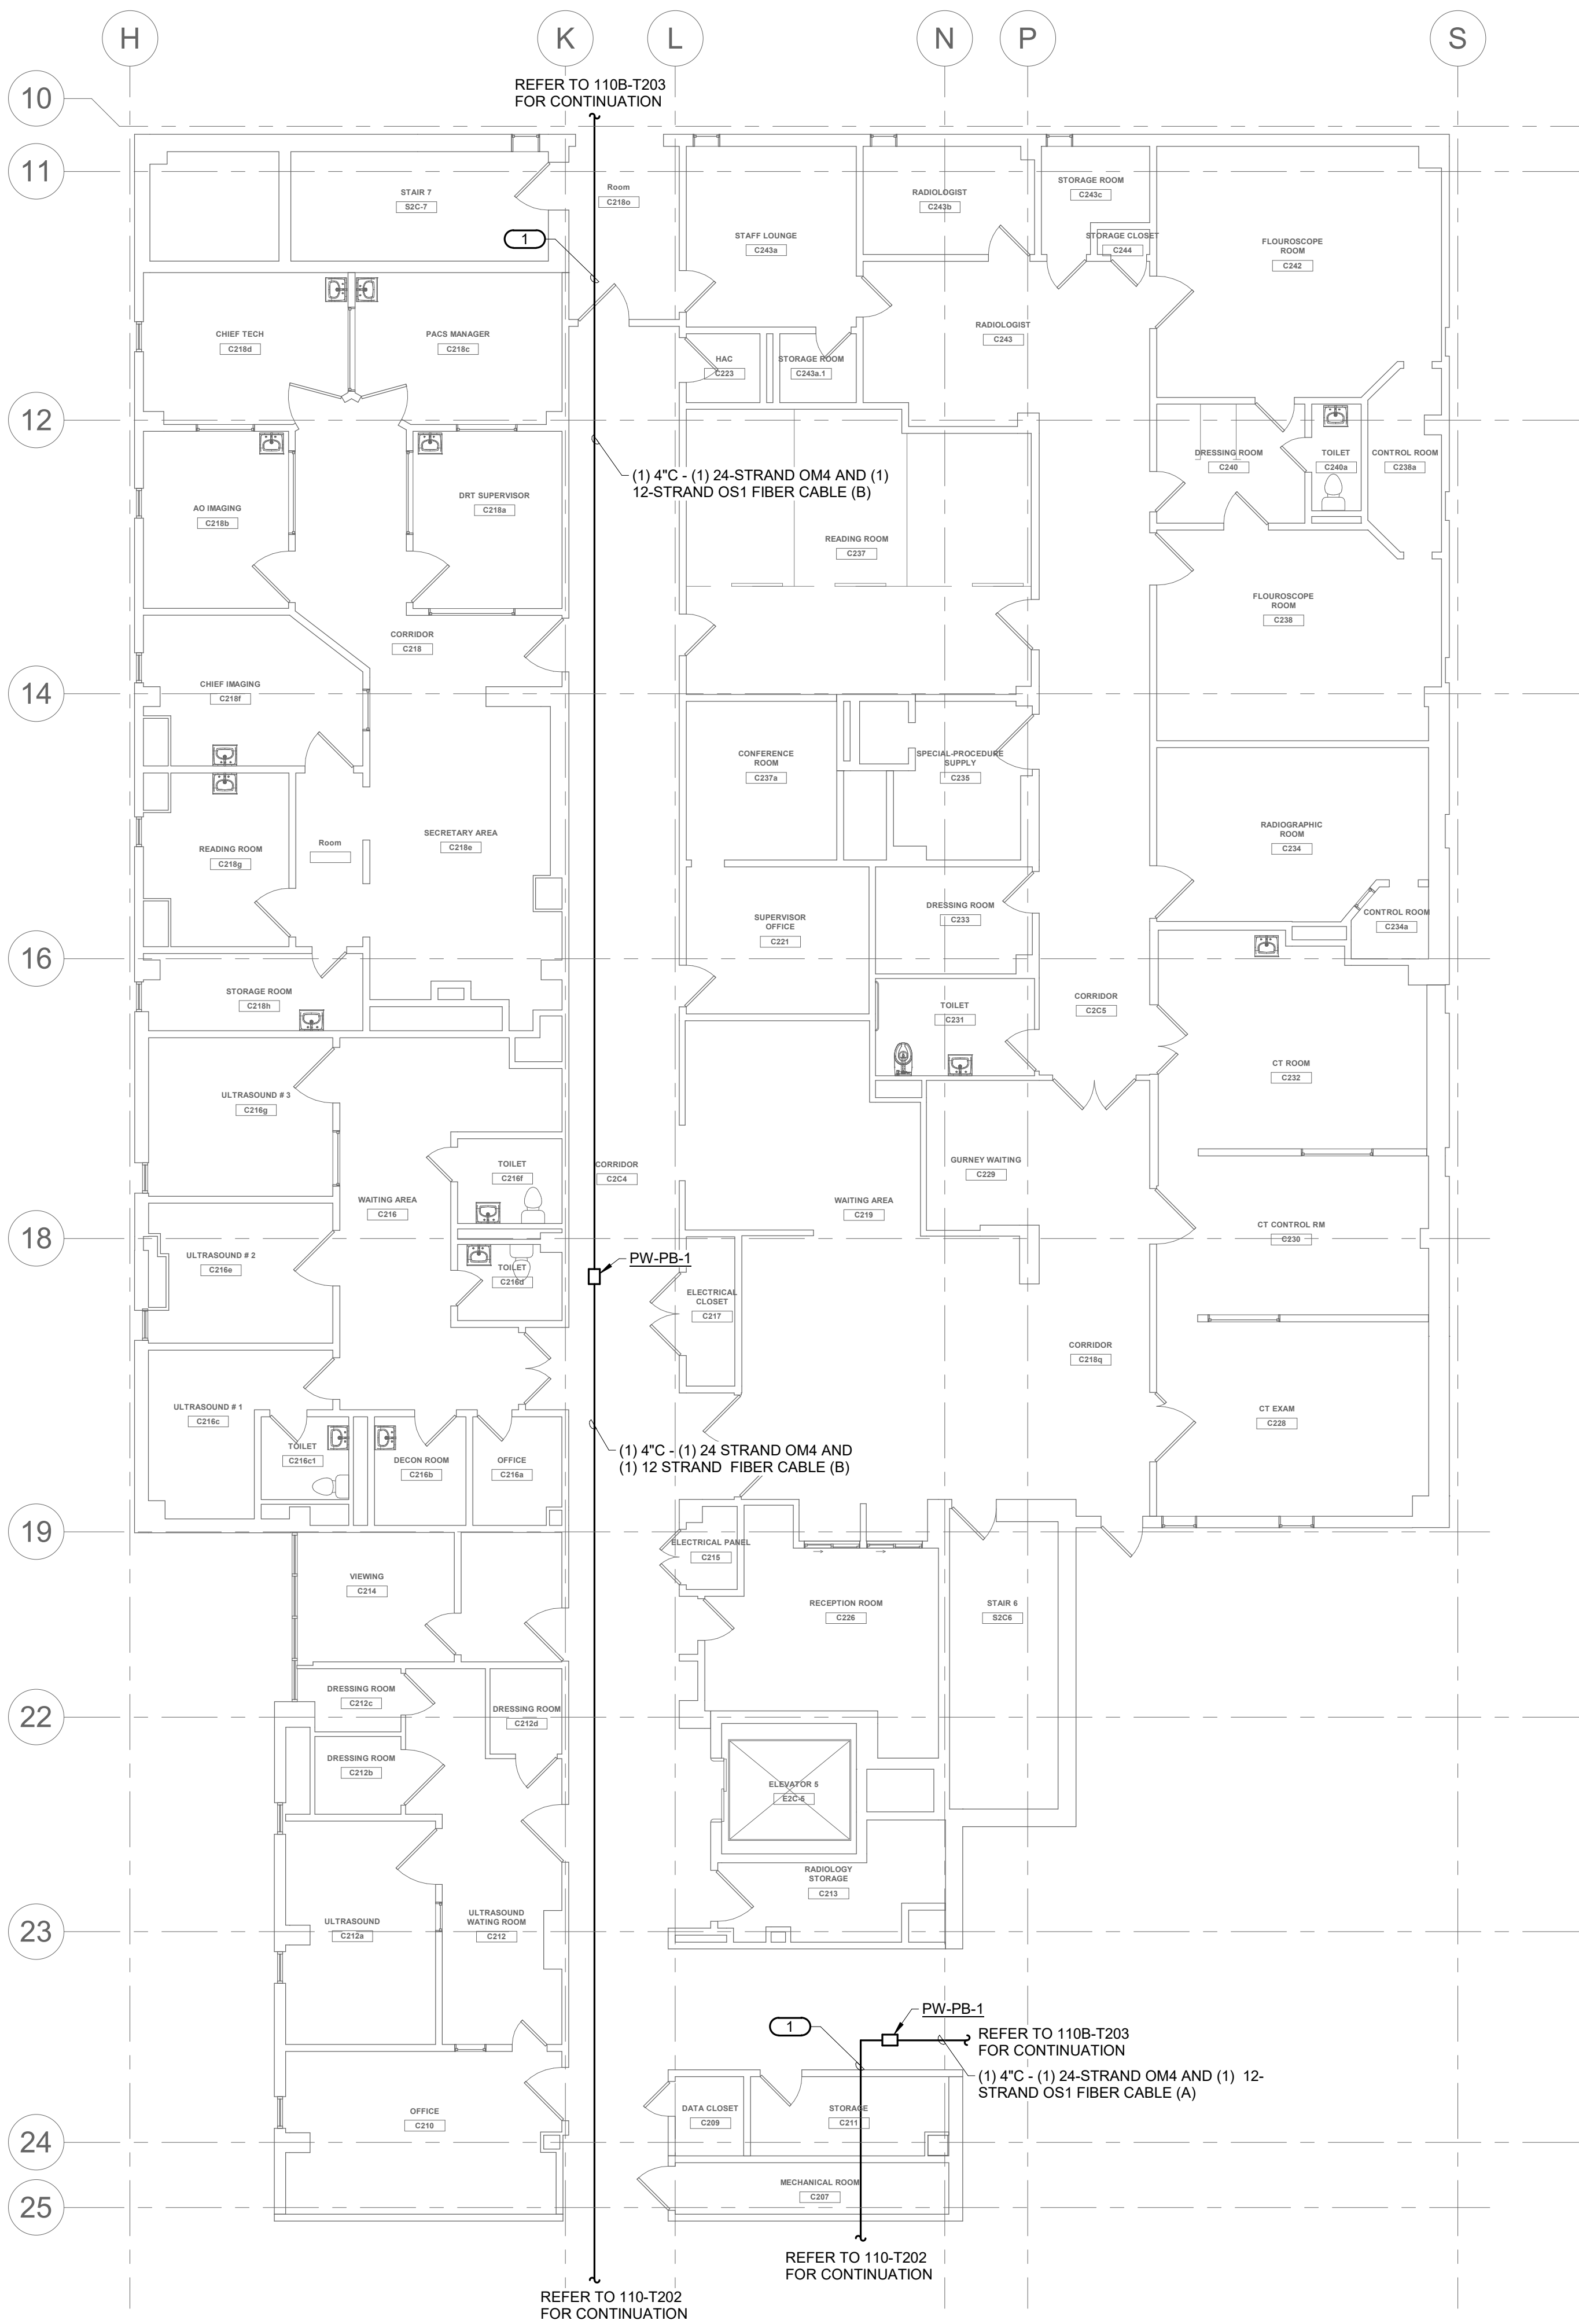


1 LEVEL 02 PLAN - TECHNOLOGY
1/8" = 1'-0"


	</
--	--	----

A
B
C
D
E
F

BM 360/509-22-700
VAHAMPTON
E:\110B\509-22-700\110B_T_021.rvt
8/2/2025 8:23:39 AM

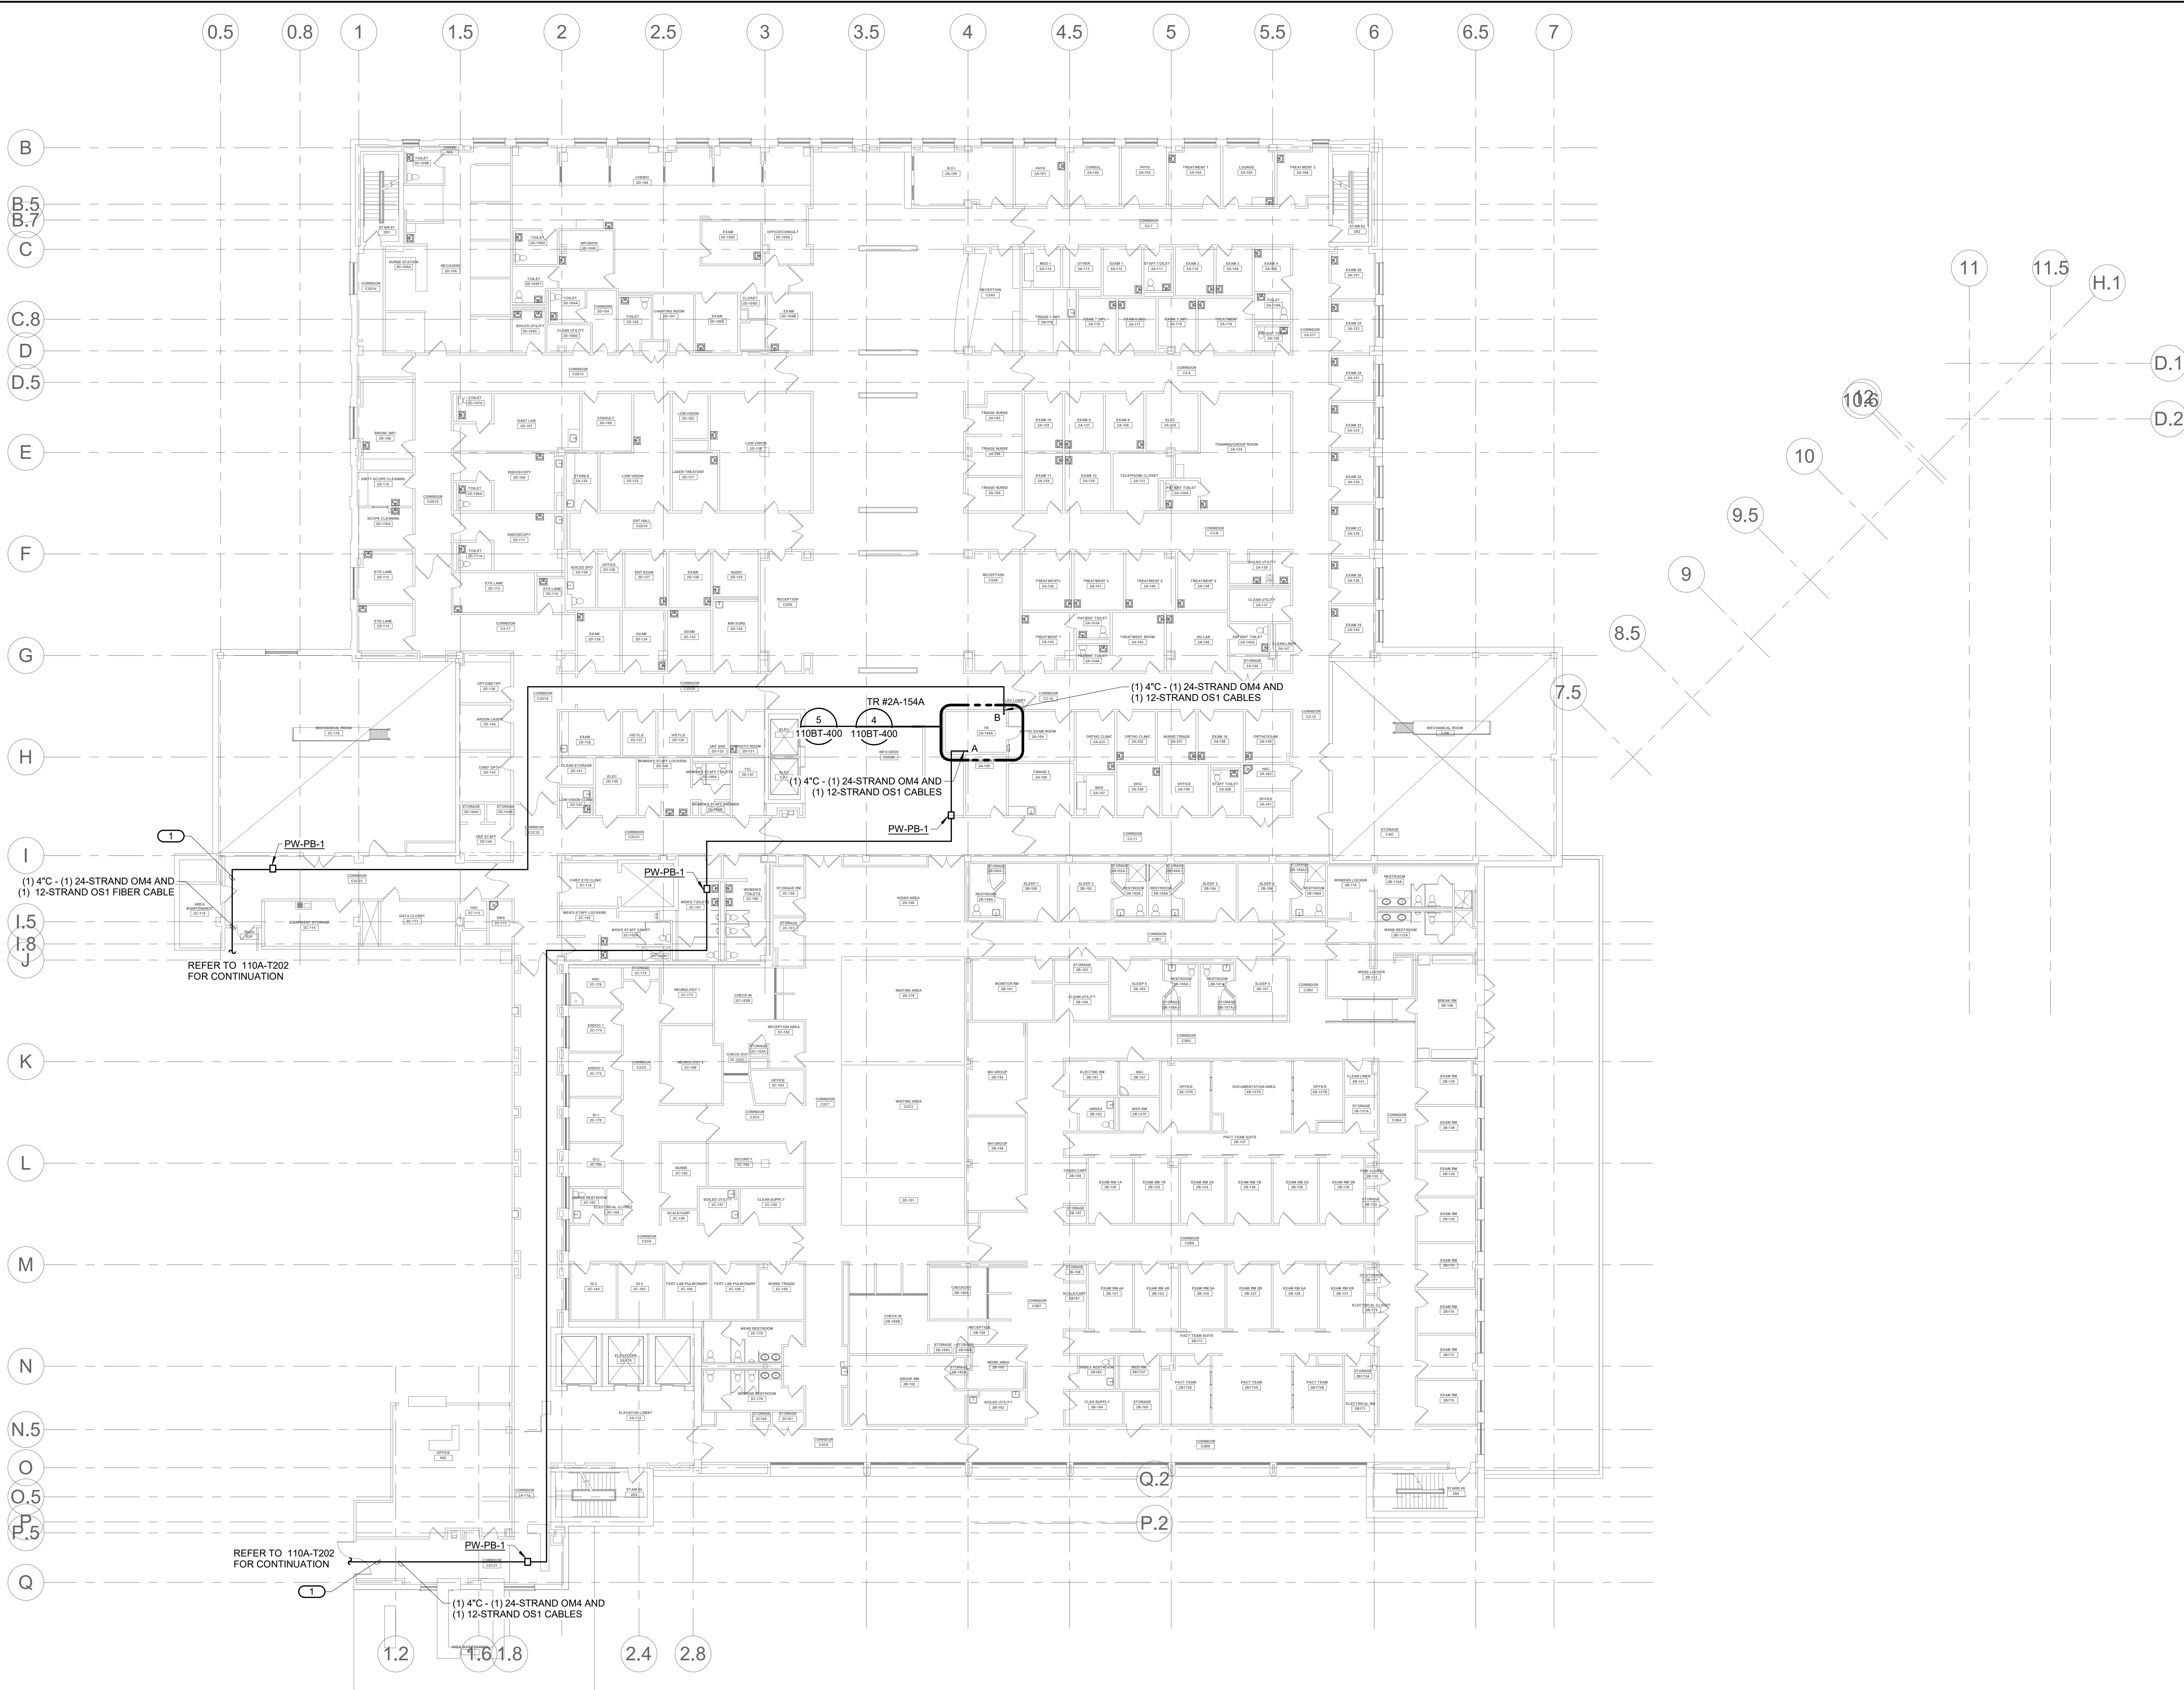


- SHEET NOTES:**
 1. REFER TO SITE PLAN TS001 FOR ADDITIONAL INFORMATION.
 2. REFER TO TS00 AND TS01 FOR CAMPUS OPTICAL FIBER RISER DIAGRAMS.
 3. REFER TO 2/7400 FOR HANDHOLE DETAIL.
 4. REFER TO ENLARGED PLANS FOR ADDITIONAL INFORMATION.
 5. ROUTES SHOWN THRU CRAWL SPACE ARE "SUGGESTED" ROUTES. FIELD VERIFY EXACT ROUTES IN CRAWL SPACE.
- KEY NOTES: C #**
 1. ROUTE CONDUITS ABOVE CORRIDOR CEILINGS TO TR # 2A-154A.
 2. ROUTE CONDUIT UP TO HEIGHT ABOVE CABLE TRAY. PROVIDE PULLBOX AND PENETRATION THRU CEILING TO ROUTE CONDUIT UP INTO TR #3C-1.TWO (2) 4\"/>

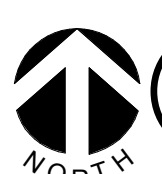 **1** **LEVEL 02 PLAN - TECHNOLOGY**
1/16" = 1'-0"

			CONSULTANT	ARCHITECT/ENGINEER OF RECORD	STAMP	Office of Construction and Facilities Management	Drawing Title	Phase	Project Title	Project Number	
			ENGINEERING DISCIPLINE:	A/E:			BLDG.110B LEVEL 02 PLAN - TECHNOLOGY	100% CONSTRUCTION DOCUMENTS	EHRM INFRASTRUCTURE UPGRADES - HAMPTON	509-22-700	
				SPEES DESIGN BUILD						Building Number	
			225 W WASHINGTON STREET	23830 PACIFIC HIGHWAY S. SUITE 203						110B	
			SUITE 2700	KENT, WA 98032			 SPEESDESIGNBUILD			Drawing Number	
Revisions:	Date:		225 W WASHINGTON STREET SUITE 2700 CHICAGO, IL 60606 P: 312.294.0501 F: 312.294.0003 PROJECT #22010109.00			U.S. Department of Veterans Affairs	FULLY SPRINKLERED	Location HAMPTON VA MEDICAL CENTER, HAMPTON, VIRGINIA	110BT-203		
								Issue Date 05/09/2025	Checked EW	Drawn IMEG	673 of 713


BM 360/509-22-700
VAHampton
E:\110B-400\110B_T_R21.rvt
8/2/2025 8:23:43 AM

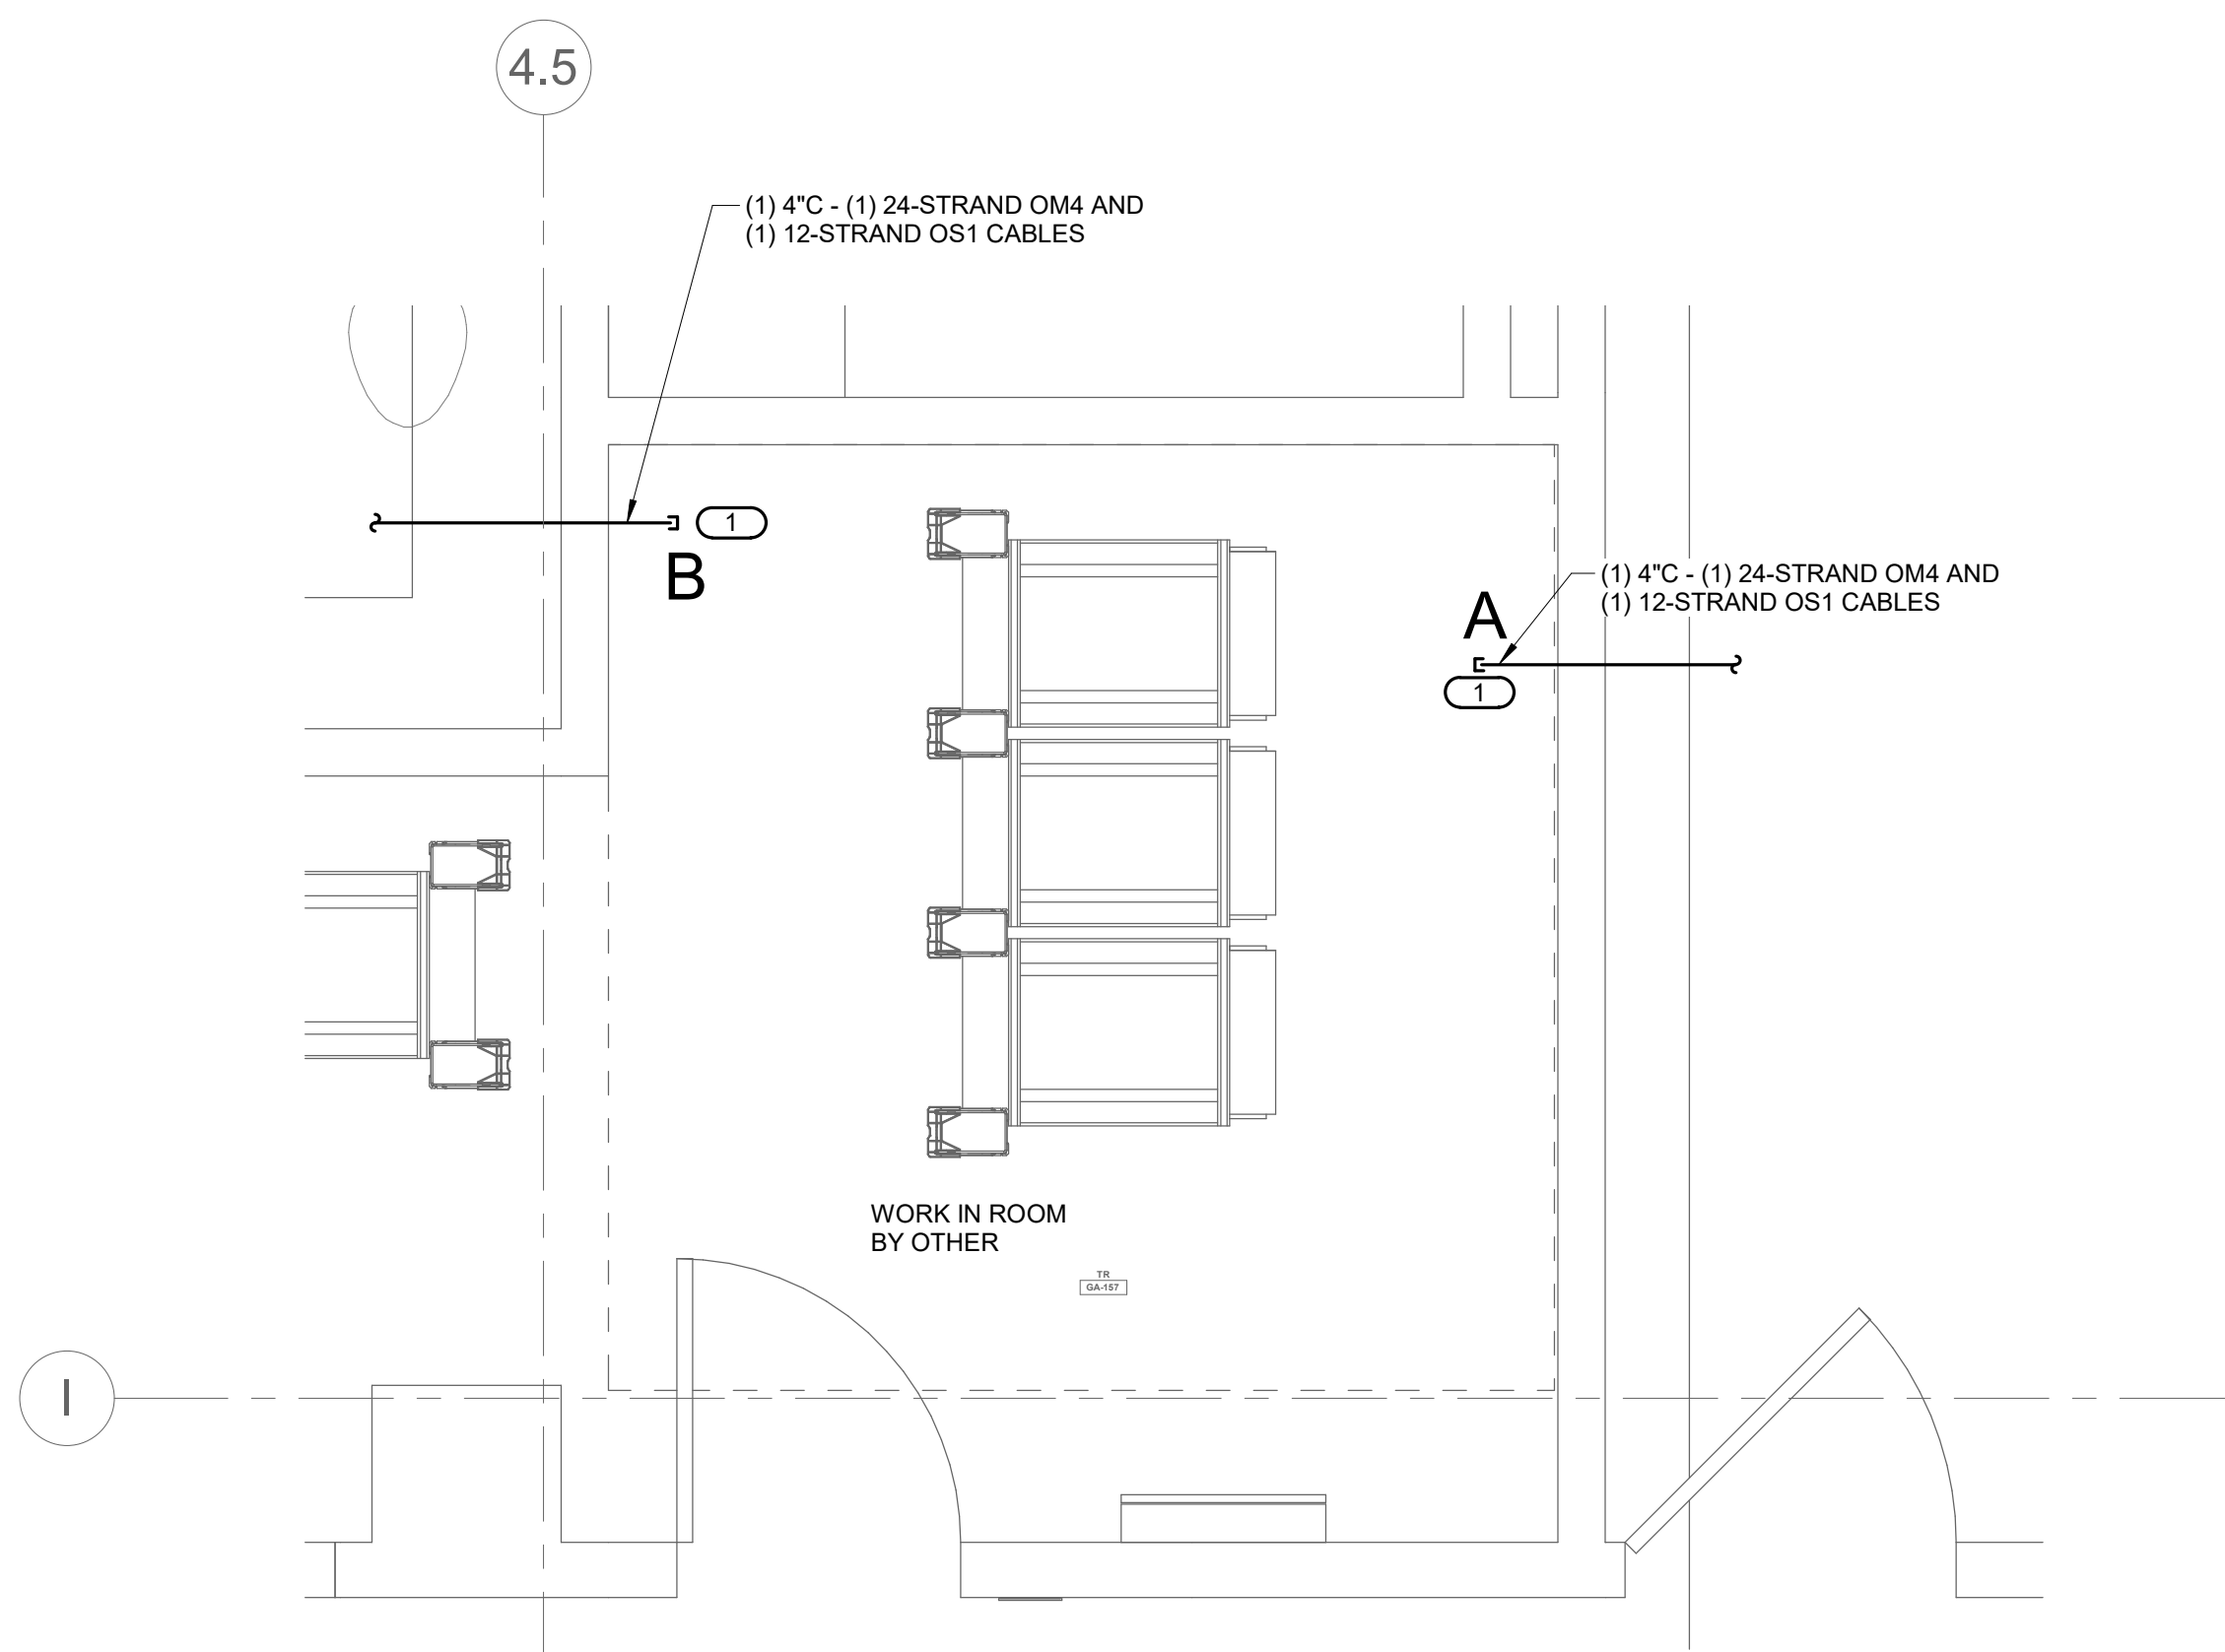


1 TELECOM ROOM ENLARGEMENT TR #GA-157
1/2" = 1'-0"

- NOTES:
1. REFER TO ELECTRICAL DRAWINGS FOR ROOM LAYOUT AND RACK ELEVATIONS.
 2. ROUTE OPTICAL FIBER CABLE TO OVERHEAD CABLE TRAY AND TERMINATE IN FIBER DISTRIBUTION CABINET.

- KEYNOTES: (B)
1. THROUGH WALL PENETRATION FOR BACKBONE CONDUIT. OPTICAL FIBER CABLE CONTINUES ON CABLE TRAY TO RACKS.

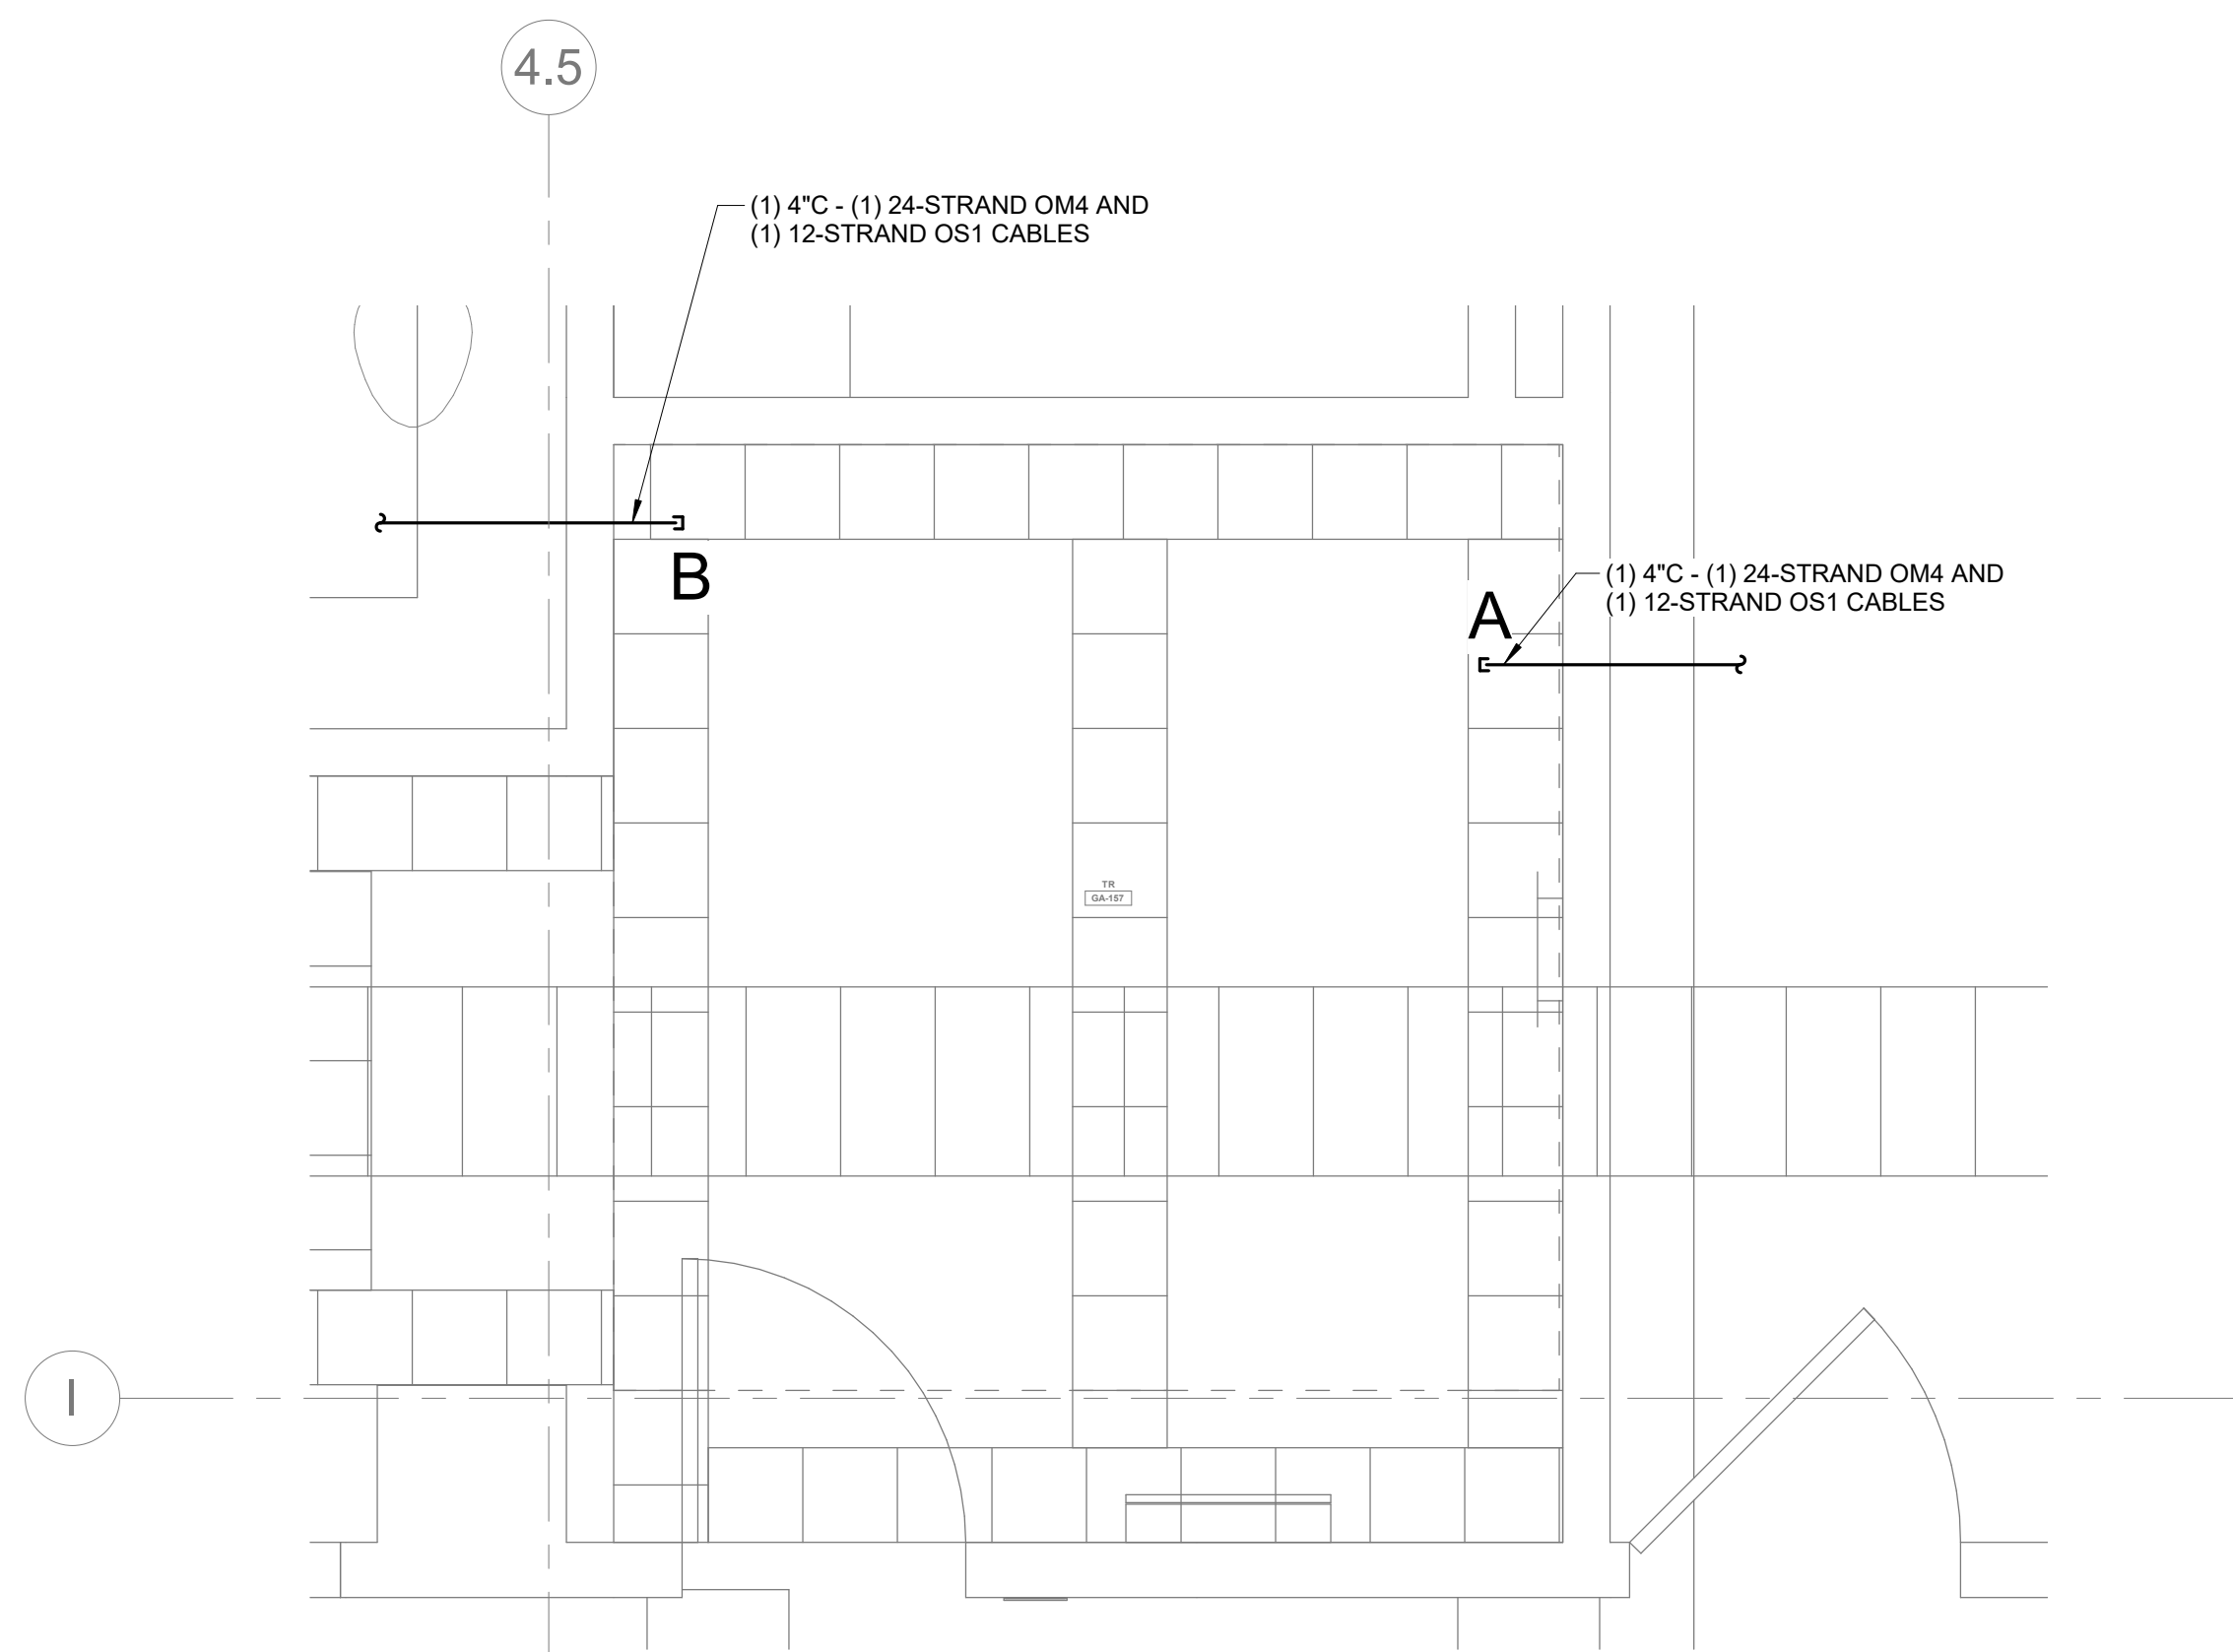


2 TELECOM ROOM PATHWAY TR #GA-157
1/2" = 1'-0"

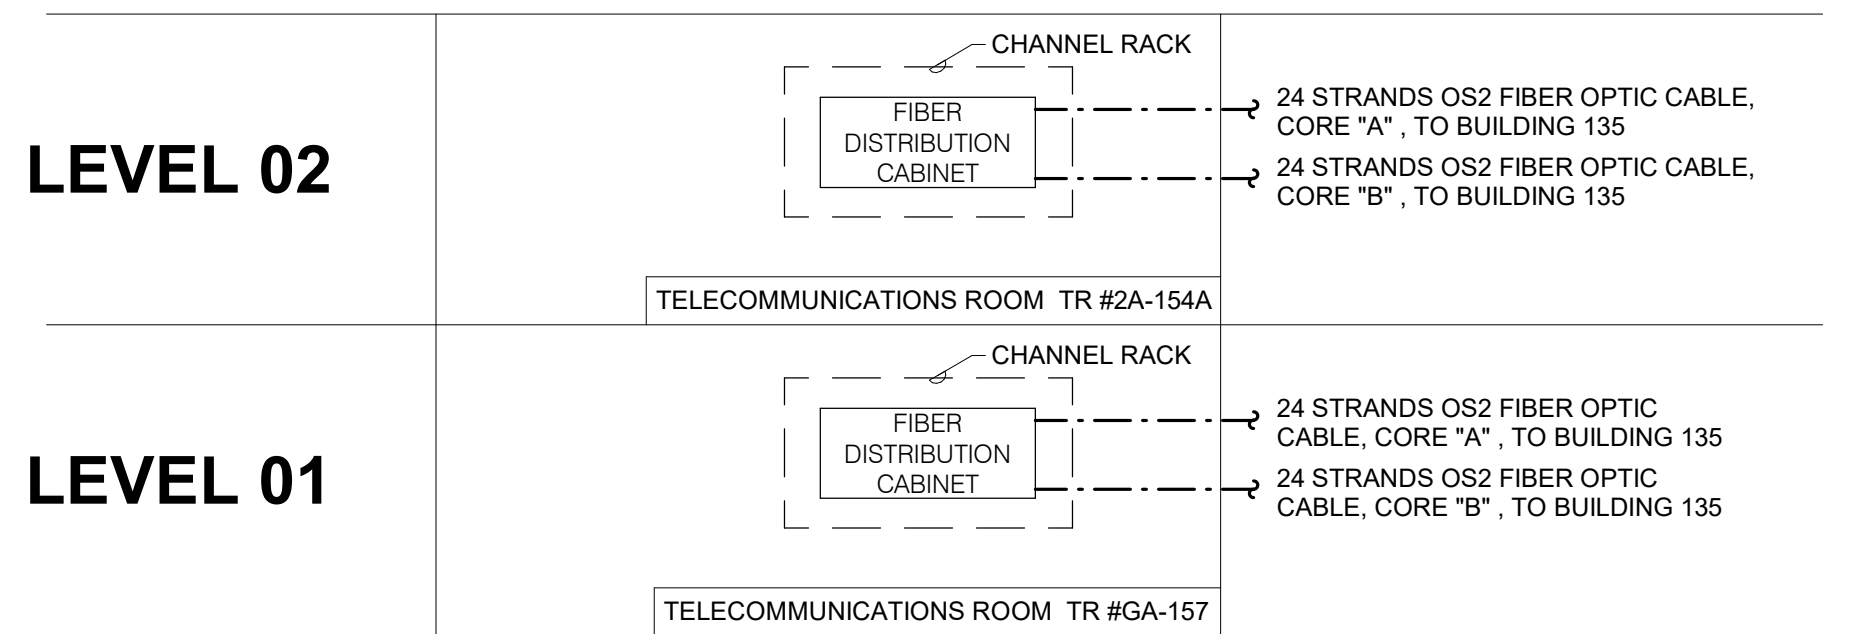

3 FIBER RISER DIAGRAM
NO SCALE


- NOTES:
1. THIS RISER IS DIAGRAMMATIC AND MAY NOT SHOW ACTUAL ROUTING OR QUANTITIES OF MATERIALS SHOWN. THIS RISER IS SHOWN FOR CLARIFICATION OF CONNECTION(S), LOCATIONS AND CABLE TYPE. ALL INFORMATION OUTLETS ARE TYPICAL OF THE OUTLETS IN THE AREA SHOWN. REFER TO FLOOR PLANS FOR MORE SPECIFIC ROUTING INFORMATION. REFER TO SPECIFICATIONS FOR ADDITIONAL REQUIREMENTS.
 2. REFER TO ELECTRICAL DRAWINGS FOR CHANNEL RACK AND FIBER OPTIC DISTRIBUTION CABINET SPECIFICATIONS.

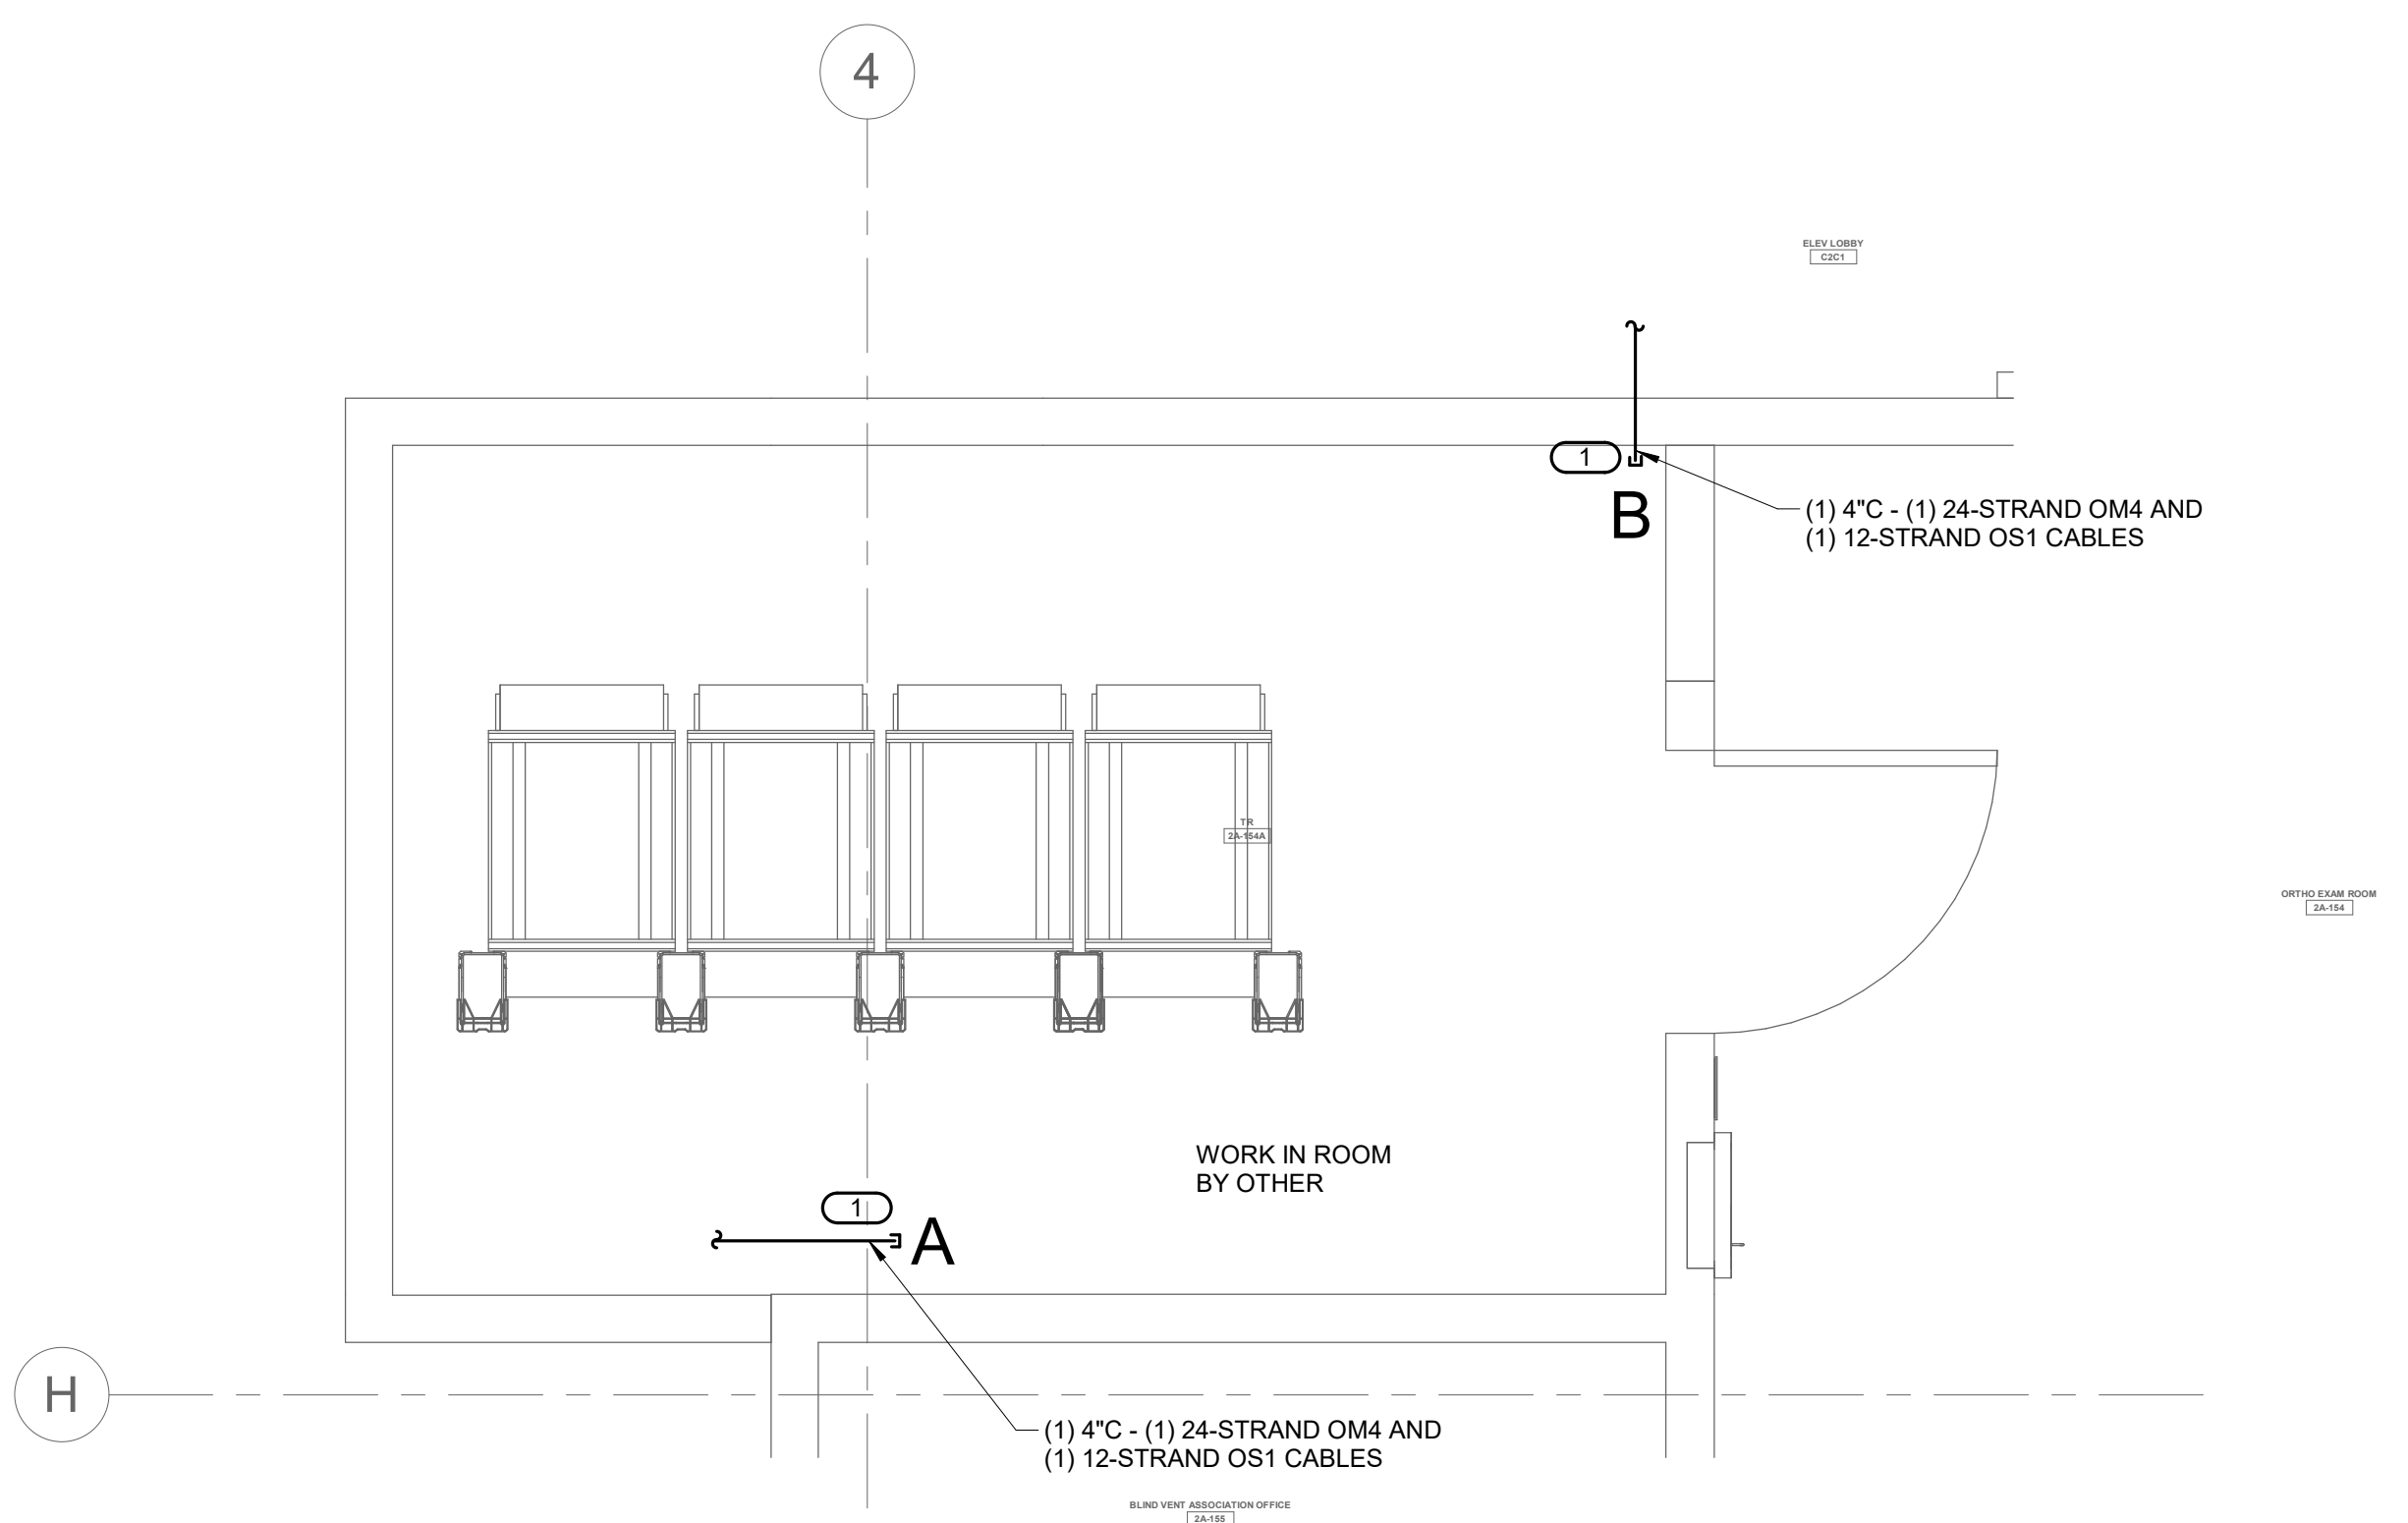


4 TELECOM ROOM ENLARGEMENT TR #2A-154A
1/2" = 1'-0"

- NOTES:
1. REFER TO ELECTRICAL DRAWINGS FOR ROOM LAYOUT AND RACK ELEVATIONS.
 2. ROUTE OPTICAL FIBER CABLE TO OVERHEAD CABLE TRAY AND TERMINATE IN FIBER DISTRIBUTION CABINET.

- KEYNOTES: (B)
1. THROUGH WALL PENETRATION FOR BACKBONE CONDUIT. OPTICAL FIBER CABLE CONTINUES ON CABLE TRAY TO RACKS.

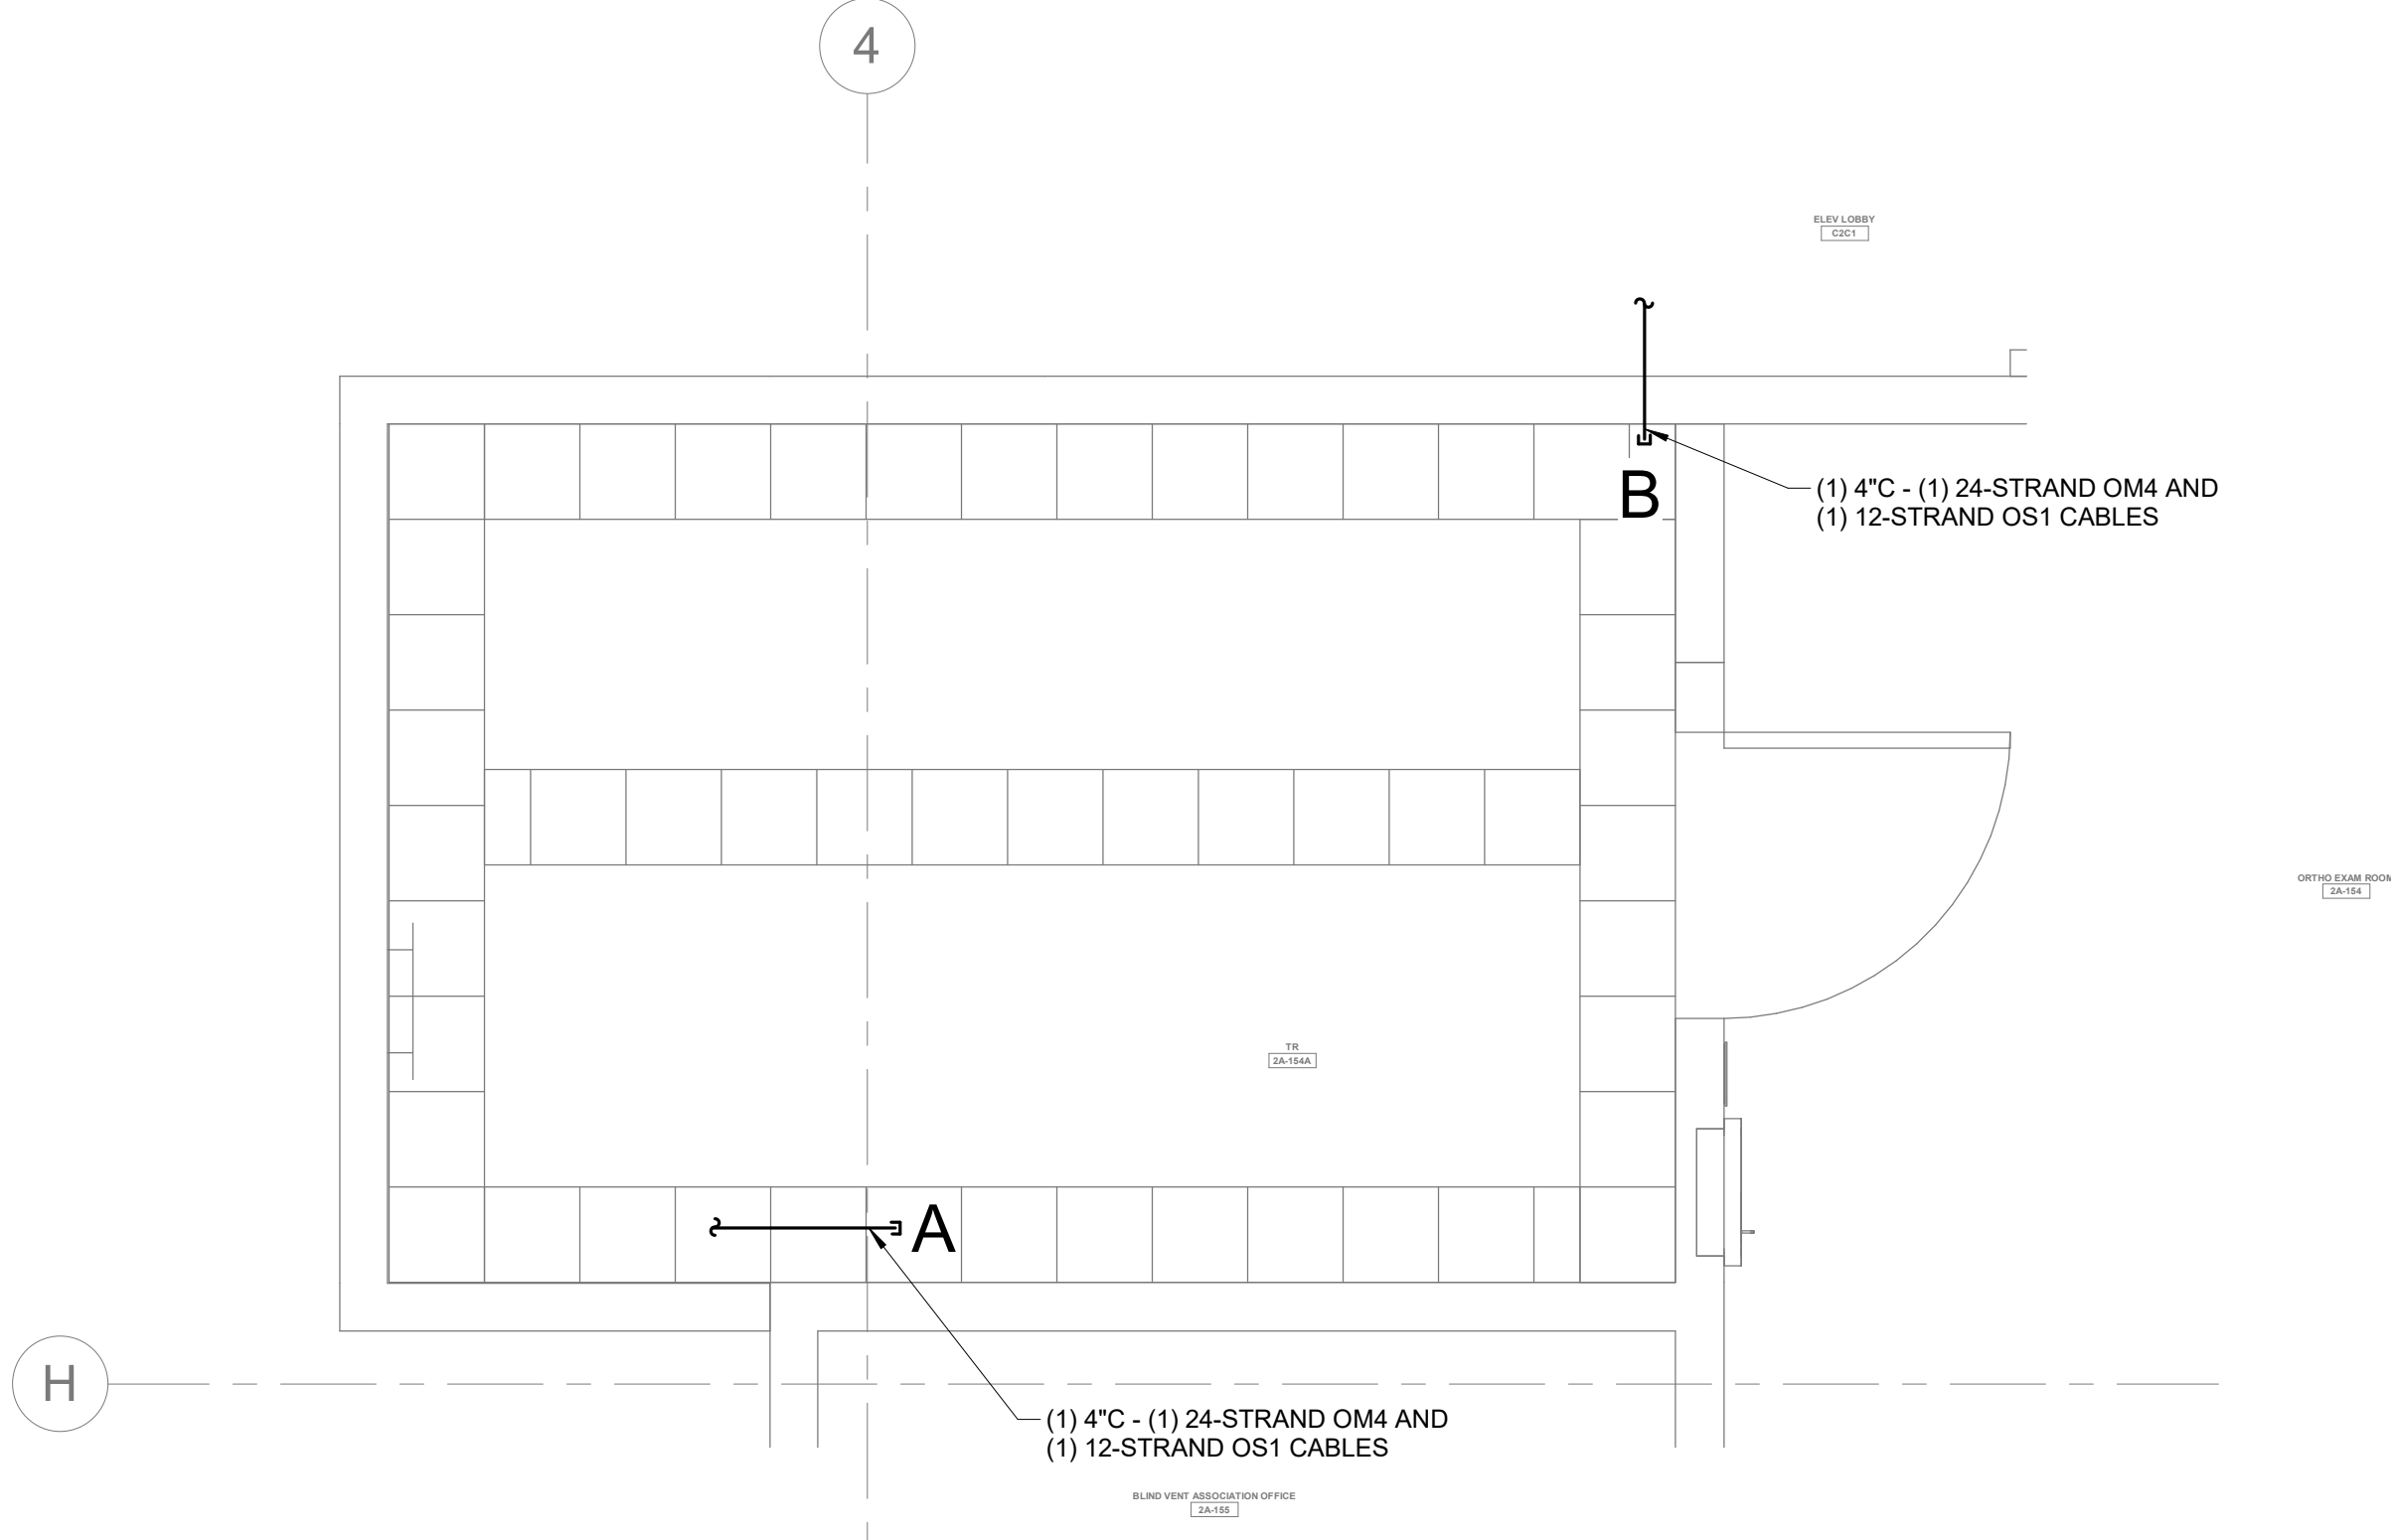

5 TELECOM ROOM PATHWAY TR #2A-154A
1/2" = 1'-0"

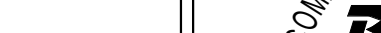	CONSULTANT		ARCHITECT/ENGINEER OF RECORD		STAMP	Office of Construction and Facilities Management	Drawing Title BLDG.110B TECHNOLOGY ENLARGED PLANS	Phase 100% CONSTRUCTION DOCUMENTS	Project Title EHRM INFRASTRUCTURE UPGRADES - HAMPTON		Project Number 509-22-700	
	ENGINEERING DISCIPLINE:		A/E:						Building Number 110B			
	 www.imegcorp.com 225 W WASHINGTON STREET SUITE 2700 CHICAGO, IL 60606 P: 312.294.0501 F: 312.294.0003 PROJECT #22010109.00		 SPEESDESIGNBUILD 23830 PACIFIC HIGHWAY S. SUITE 203 KENT, WA 98032						Drawing Number 110BT-400			
	Revisions:		Date:						110BT-400			
	Issue Date 05/09/2025		Checked EW						Drawn IMEG		674 of 713	

A


B

C

D

E

F

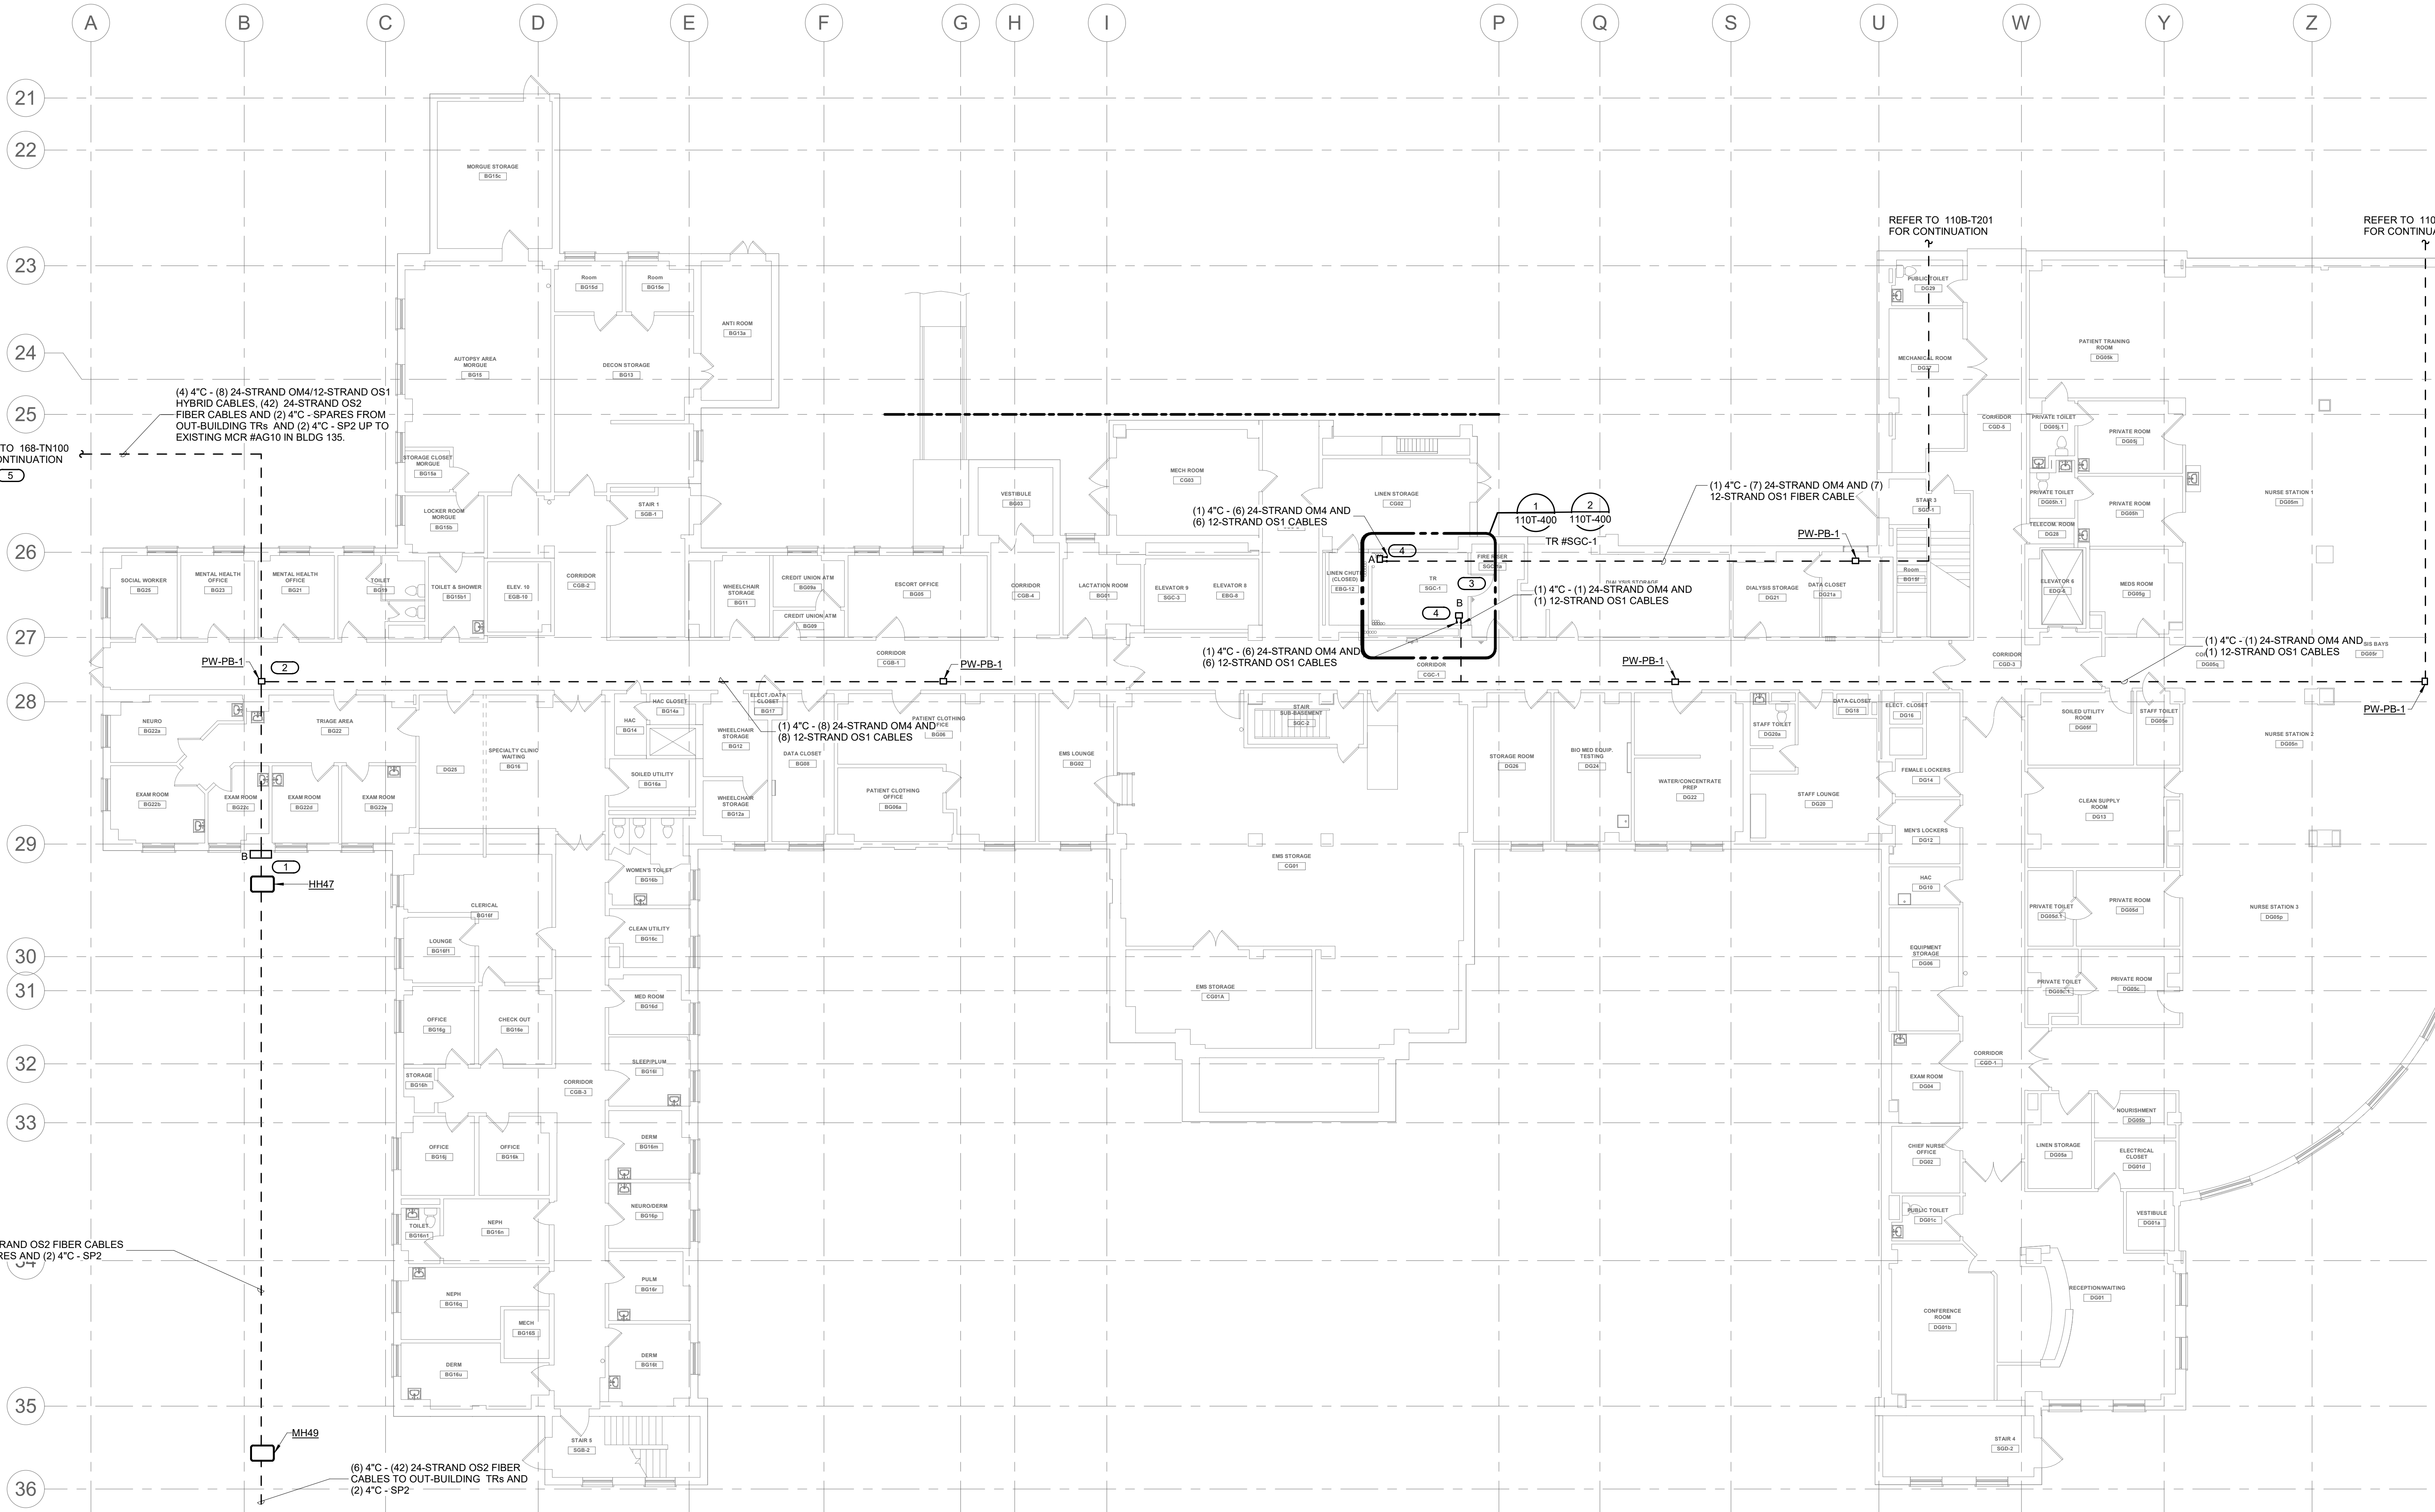

- SHEET NOTES:**
1. REFER TO SITEPLAN TS001 FOR ADDITIONAL INFORMATION.
 2. REFER TO TS00 AND TS01 FOR CAMPUS OPTICAL FIBER RISER DIAGRAMS.
 3. REFER TO 2/T400 FOR HANDHOLE DETAIL.
 4. REFER TO ENLARGED PLANS FOR ADDITIONAL INFORMATION.
 5. ROUTES SHOWN THRU CRAWL SPACE ARE "SUGGESTED" ROUTES. FIELD VERIFY EXACT ROUTES IN CRAWL SPACE.
- KEY NOTES: (#)**
1. PROVIDE PENETRATION THRU EXTERIOR WALL AND ROUTE CONDUITS INTO BLDG. 110 CRAWL SPACE.
 2. PROVIDE PULLBOX TO SEPARATE CONDUITS GOING TO BLDG 110 TRs AND CONDUITS GOING TO EXISTING MCR #AG10 IN BLDG 135.
 3. CONTINUE ROUTE OF CONDUITS/CABLES IN CRAWLS SPACE OF BLDG 110 TO LOCATIONS BELOW BASEMENT LEVEL TRs #SGC-1. PROVIDE PENETRATIONS THRU CEILING DECK AND ROUTE CONDUITS UP INTO TRs.
 4. CONTINUE ROUTE OF CONDUITS UP TO HEIGHT ABOVE CABLE TRAY IN TR #SGC-1. PROVIDE PULLBOX AT CEILING HEIGHT AND PENETRATIONS THRU CEILING DECK TO CONTINUE ROUTE TO STACK TR AT FLOORS ABOVE.
 5. PROVIDE PENETRATIONS THRU WALL OF BLDG 168 AND CONTINUE ROUTE OF CONDUITS INTO CRAWL SPACE OF BLDG 168. REFER TO BLDG #168 TECHNOLOGY PLANS FOR CONTINUED ROUTE OF CONDUITS AND CORE B OPTICAL FIBER CABLES UP TO EXISTING MCR IN BLDG 135.

A

B

C

D


E

F

1 BASEMENT PLAN - TECHNOLOGY
1" = 10'-0"

--	--	

- SHEET NOTES:
1. REFER TO ENLARGED PLANS FOR ADDITIONAL INFORMATION.
- KEY NOTES: (#)
1. ROUTE CONDUIT UP TO HEIGHT ABOVE CABLE TRAY. PROVIDE PULLBOX AND PENETRATION THRU CEILING TO ROUTE CONDUIT UP INTO TR #S2C-1.

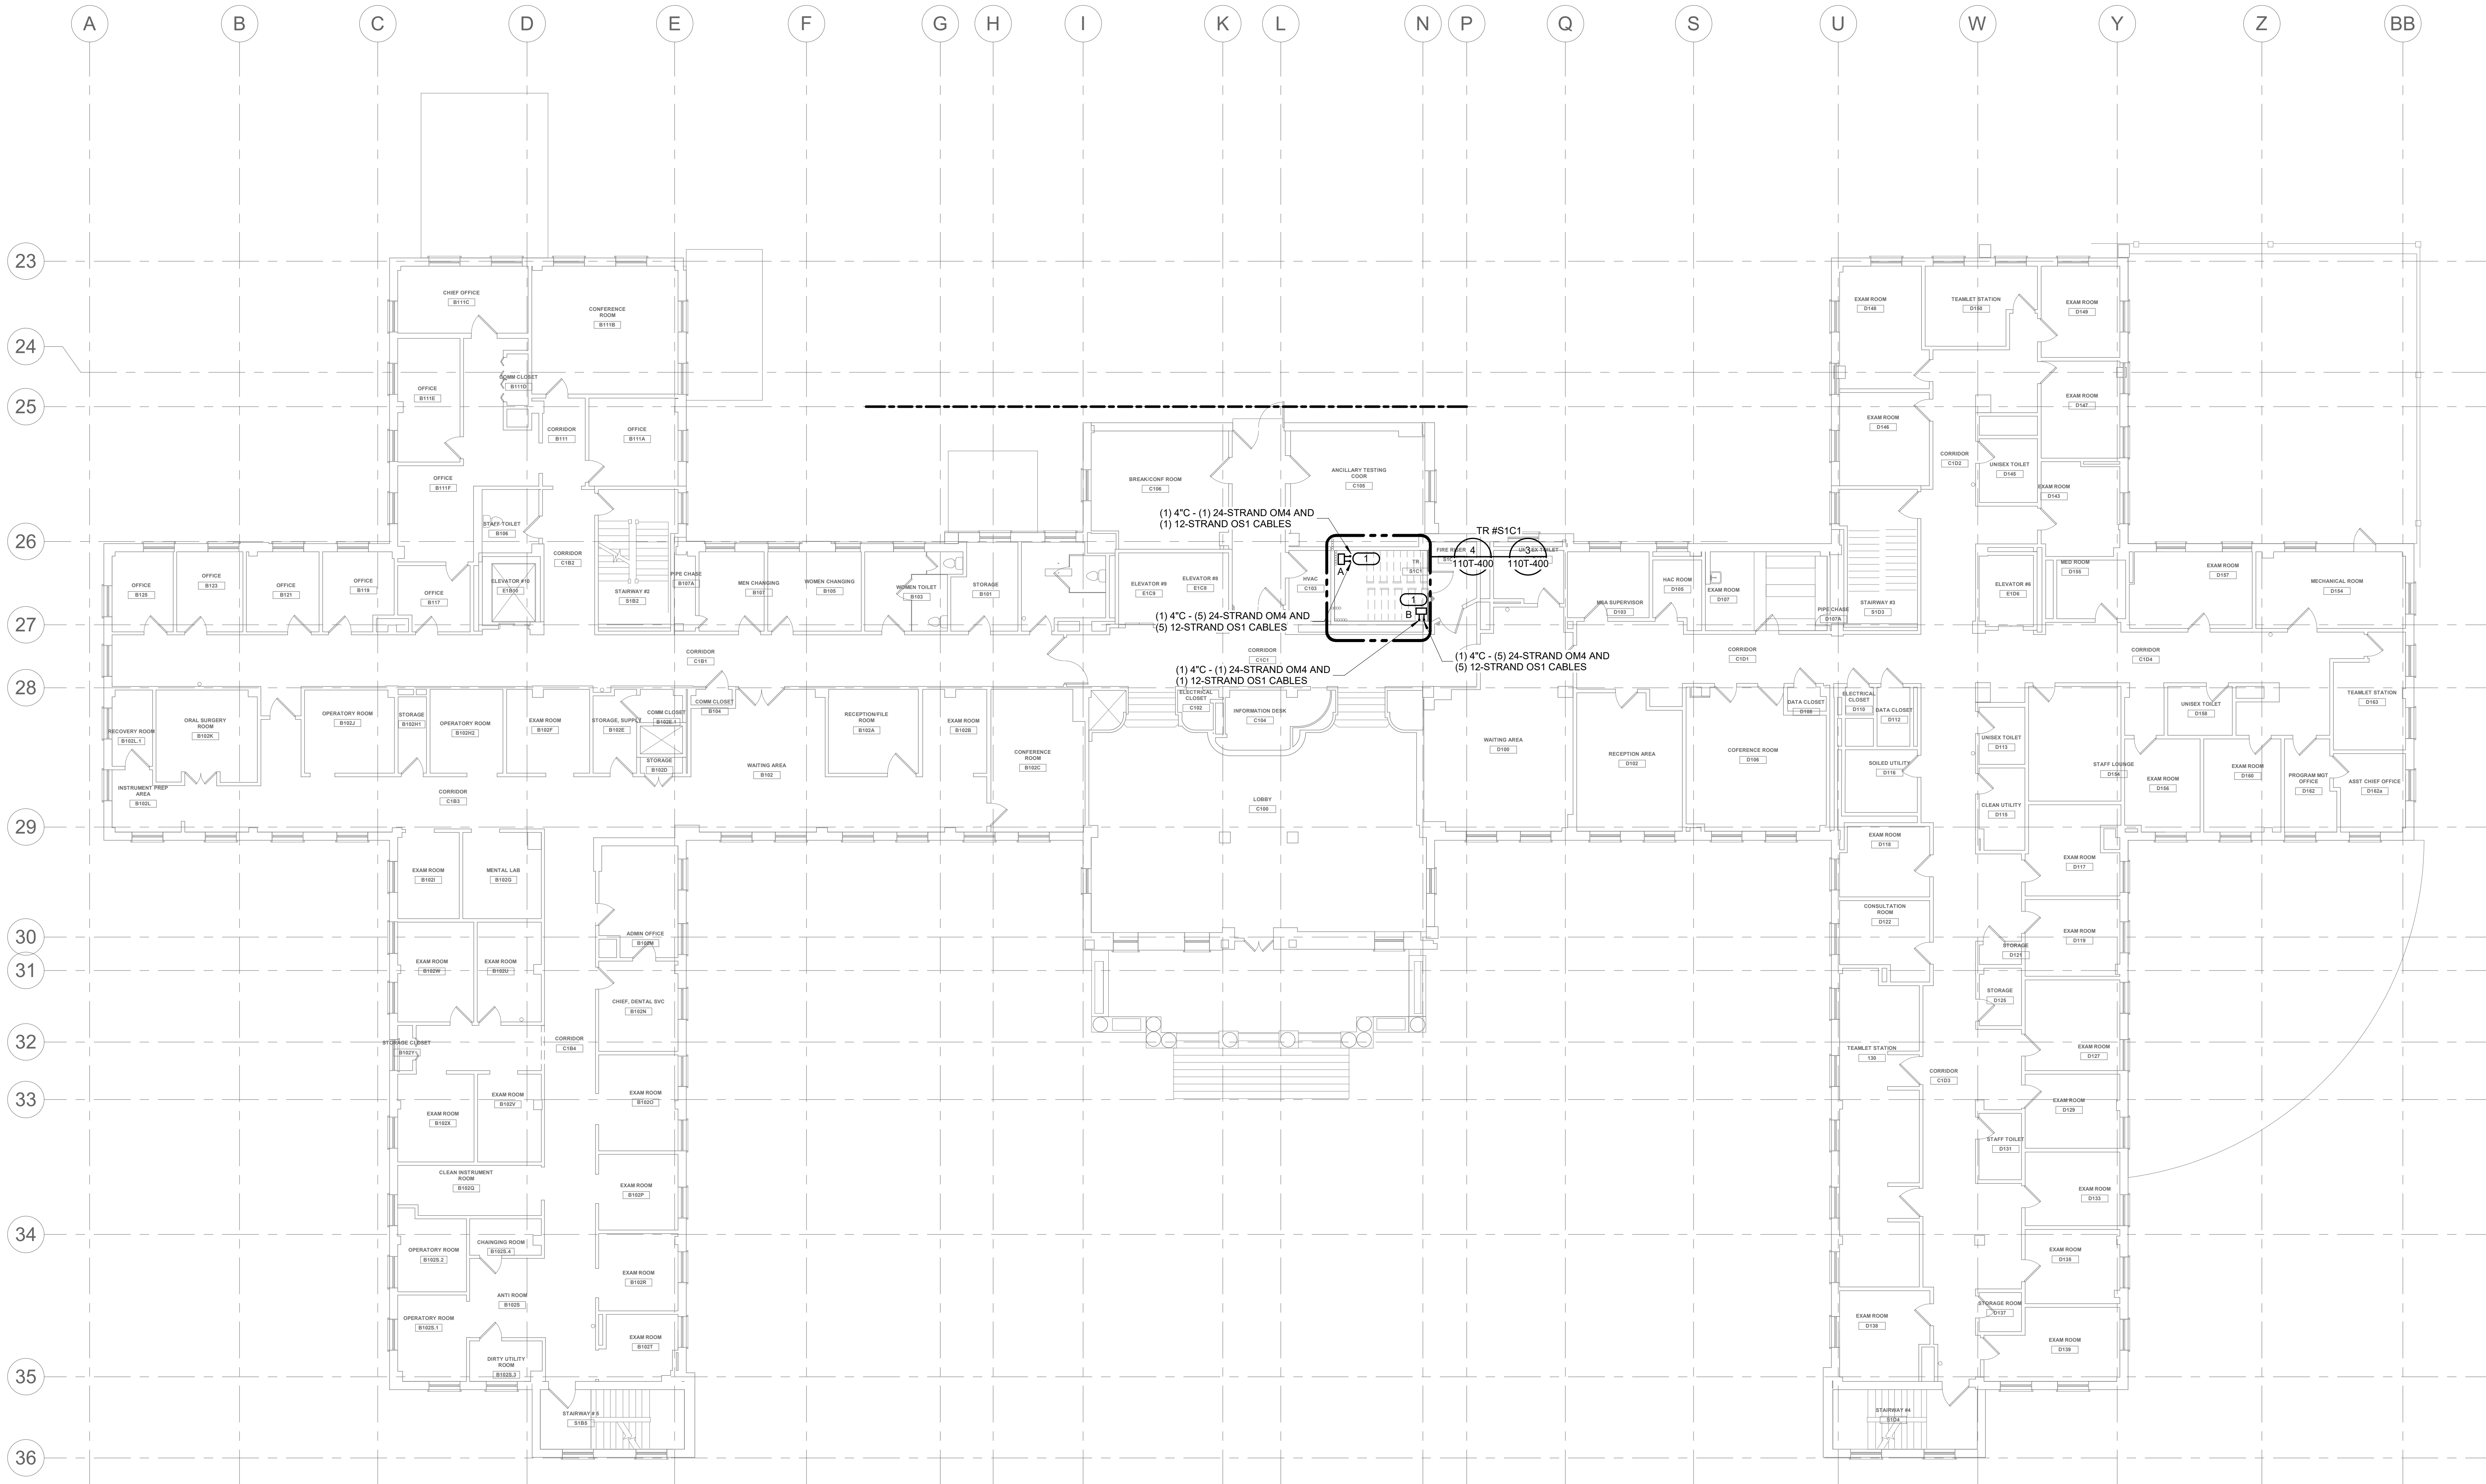

1 LEVEL 01 PLAN - TECHNOLOGY
1" = 10'-0"

	</
--	--	----

A

B


C

D

E

F

- SHEET NOTES:**
1. REFER TO SITEPLAN TS001 FOR ADDITIONAL INFORMATION.
 2. REFER TO TS00 AND 00-TS01 FOR CAMPUS OPTICAL FIBER RISER DIAGRAMS.
 3. REFER TO 2/1400 FOR HANDHOLE DETAIL.
 4. REFER TO ENLARGED PLANS FOR ADDITIONAL INFORMATION.
 5. ROUTES SHOWN THRU CRAWL SPACE ARE "SUGGESTED" ROUTES. FIELD VERIFY EXACT ROUTES IN CRAWL SPACE.
- KEY NOTES:**
1. ROUTE CONDUIT UP TO HEIGHT ABOVE CABLE TRAY. PROVIDE PULLBOX AND EXTEND CONDUIT THRU CORRIDOR TO TR #2A-154A.
 2. PROVIDE PENETRATION THRU CEILING AND ADDITIONAL CONDUIT FROM PULLBOX AND ROUTE CONDUIT UP INTO TR #S3C-1.

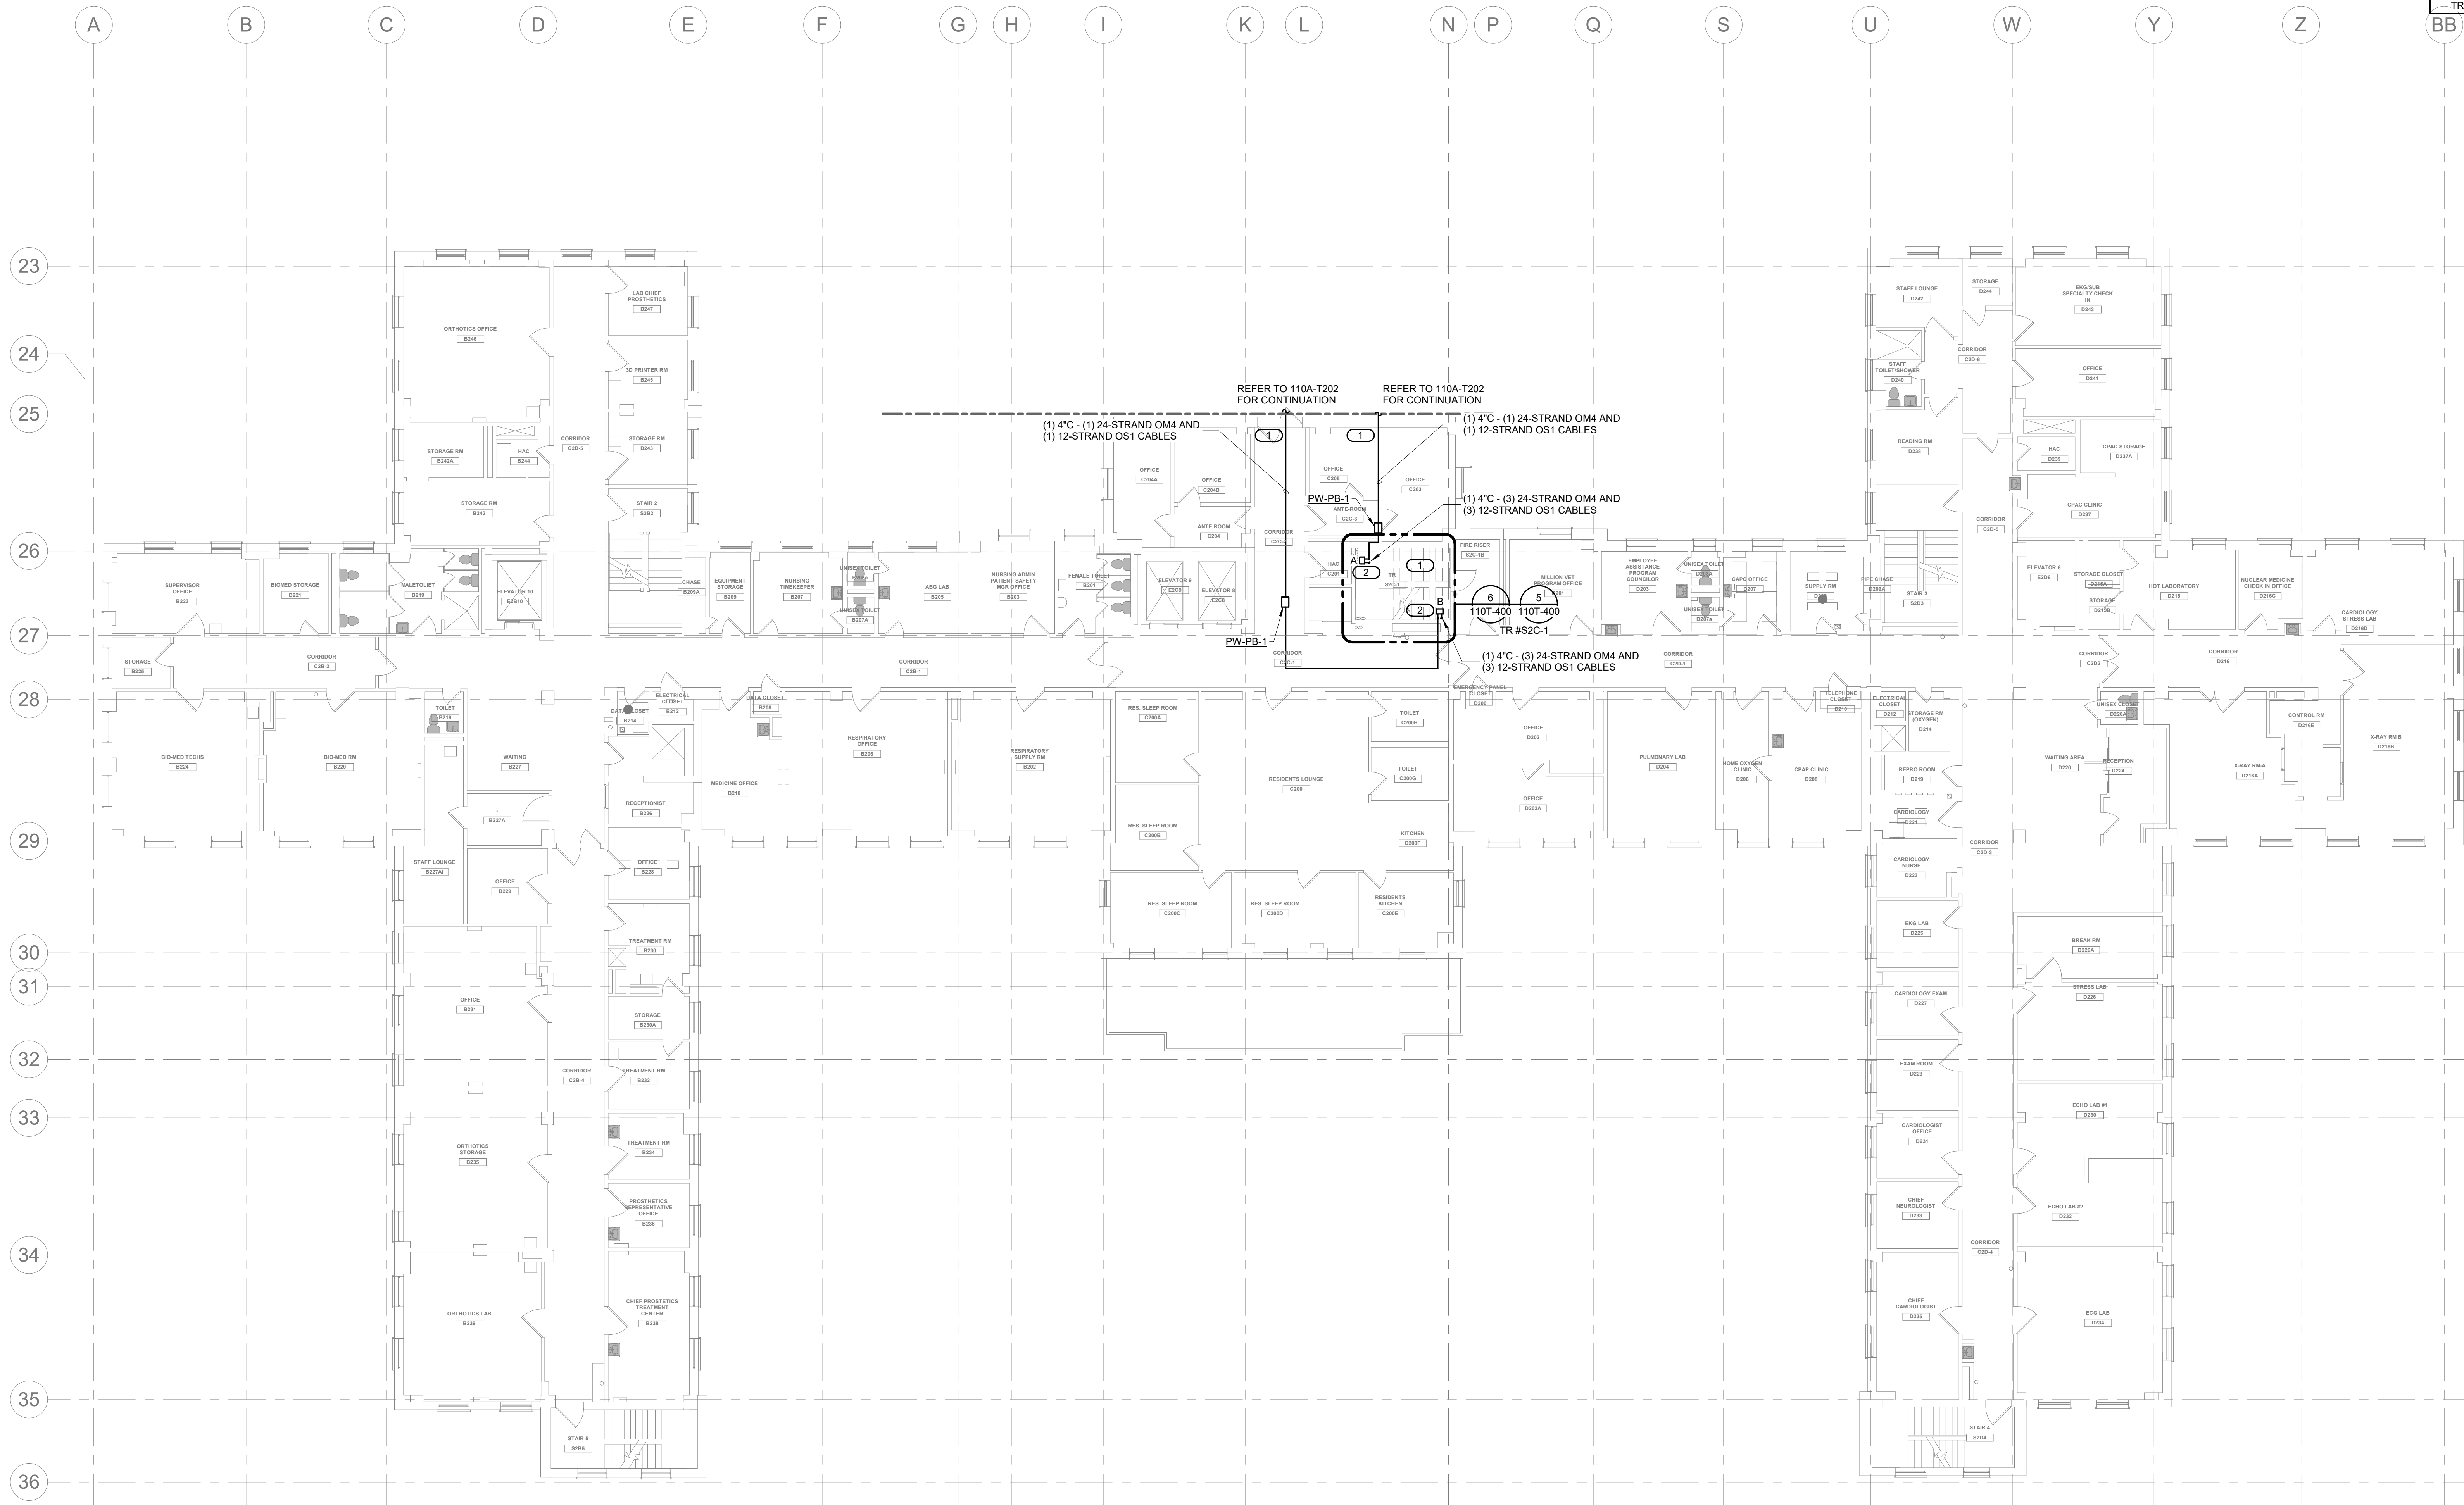

LEVEL 02 PLAN - TECHNOLOGY

1" = 10'-0"

Revisions:	Date:

CONSULTANT
ENGINEERING DISCIPLINE:
IMEG
www.imegcorp.com
225 W WASHINGTON STREET
SUITE 2700
CHICAGO, IL 60606
P: 312.294.0501 F: 312.294.0003
PROJECT #22010109.00

ARCHITECT/ENGINEER OF RECORD
A/E:
SPEES DESIGN BUILD
23830 PACIFIC HIGHWAY S. SUITE 203
KENT, WA 98032
SDB SPEESDESIGNBUILD

STAMP
Bicsi
COMMUNICATIONS DISTRIBUTION DESIGNER
Reg. No. 159309
Expires 03-01-2025
RCDD

Office of
Construction
and Facilities
Management
VA U.S. Department
of Veterans Affairs



Drawing Title
BLDG.110 LEVEL 02 PLAN - TECHNOLOGY
Approved:

Phase
100% CONSTRUCTION
DOCUMENTS
FULLY SPRINKLERED

Project Title
EHRM INFRASTRUCTURE
UPGRADES - HAMPTON
Location
HAMPTON VA MEDICAL CENTER, HAMPTON, VIRGINIA
Issue Date
05/09/2025
Checked
EW
Drawn
IMEG

Project Number
509-22-700
Building Number
110
Drawing Number
110T-202
677 of 713


1. ROUTE CONDUIT UP TO HEIGHT ABOVE CABLE TRAY. PROVIDE PULLBOX AND PENETRATION THRU CEILING TO ROUTE CONDUIT UP INTO TR #S4D-1.

 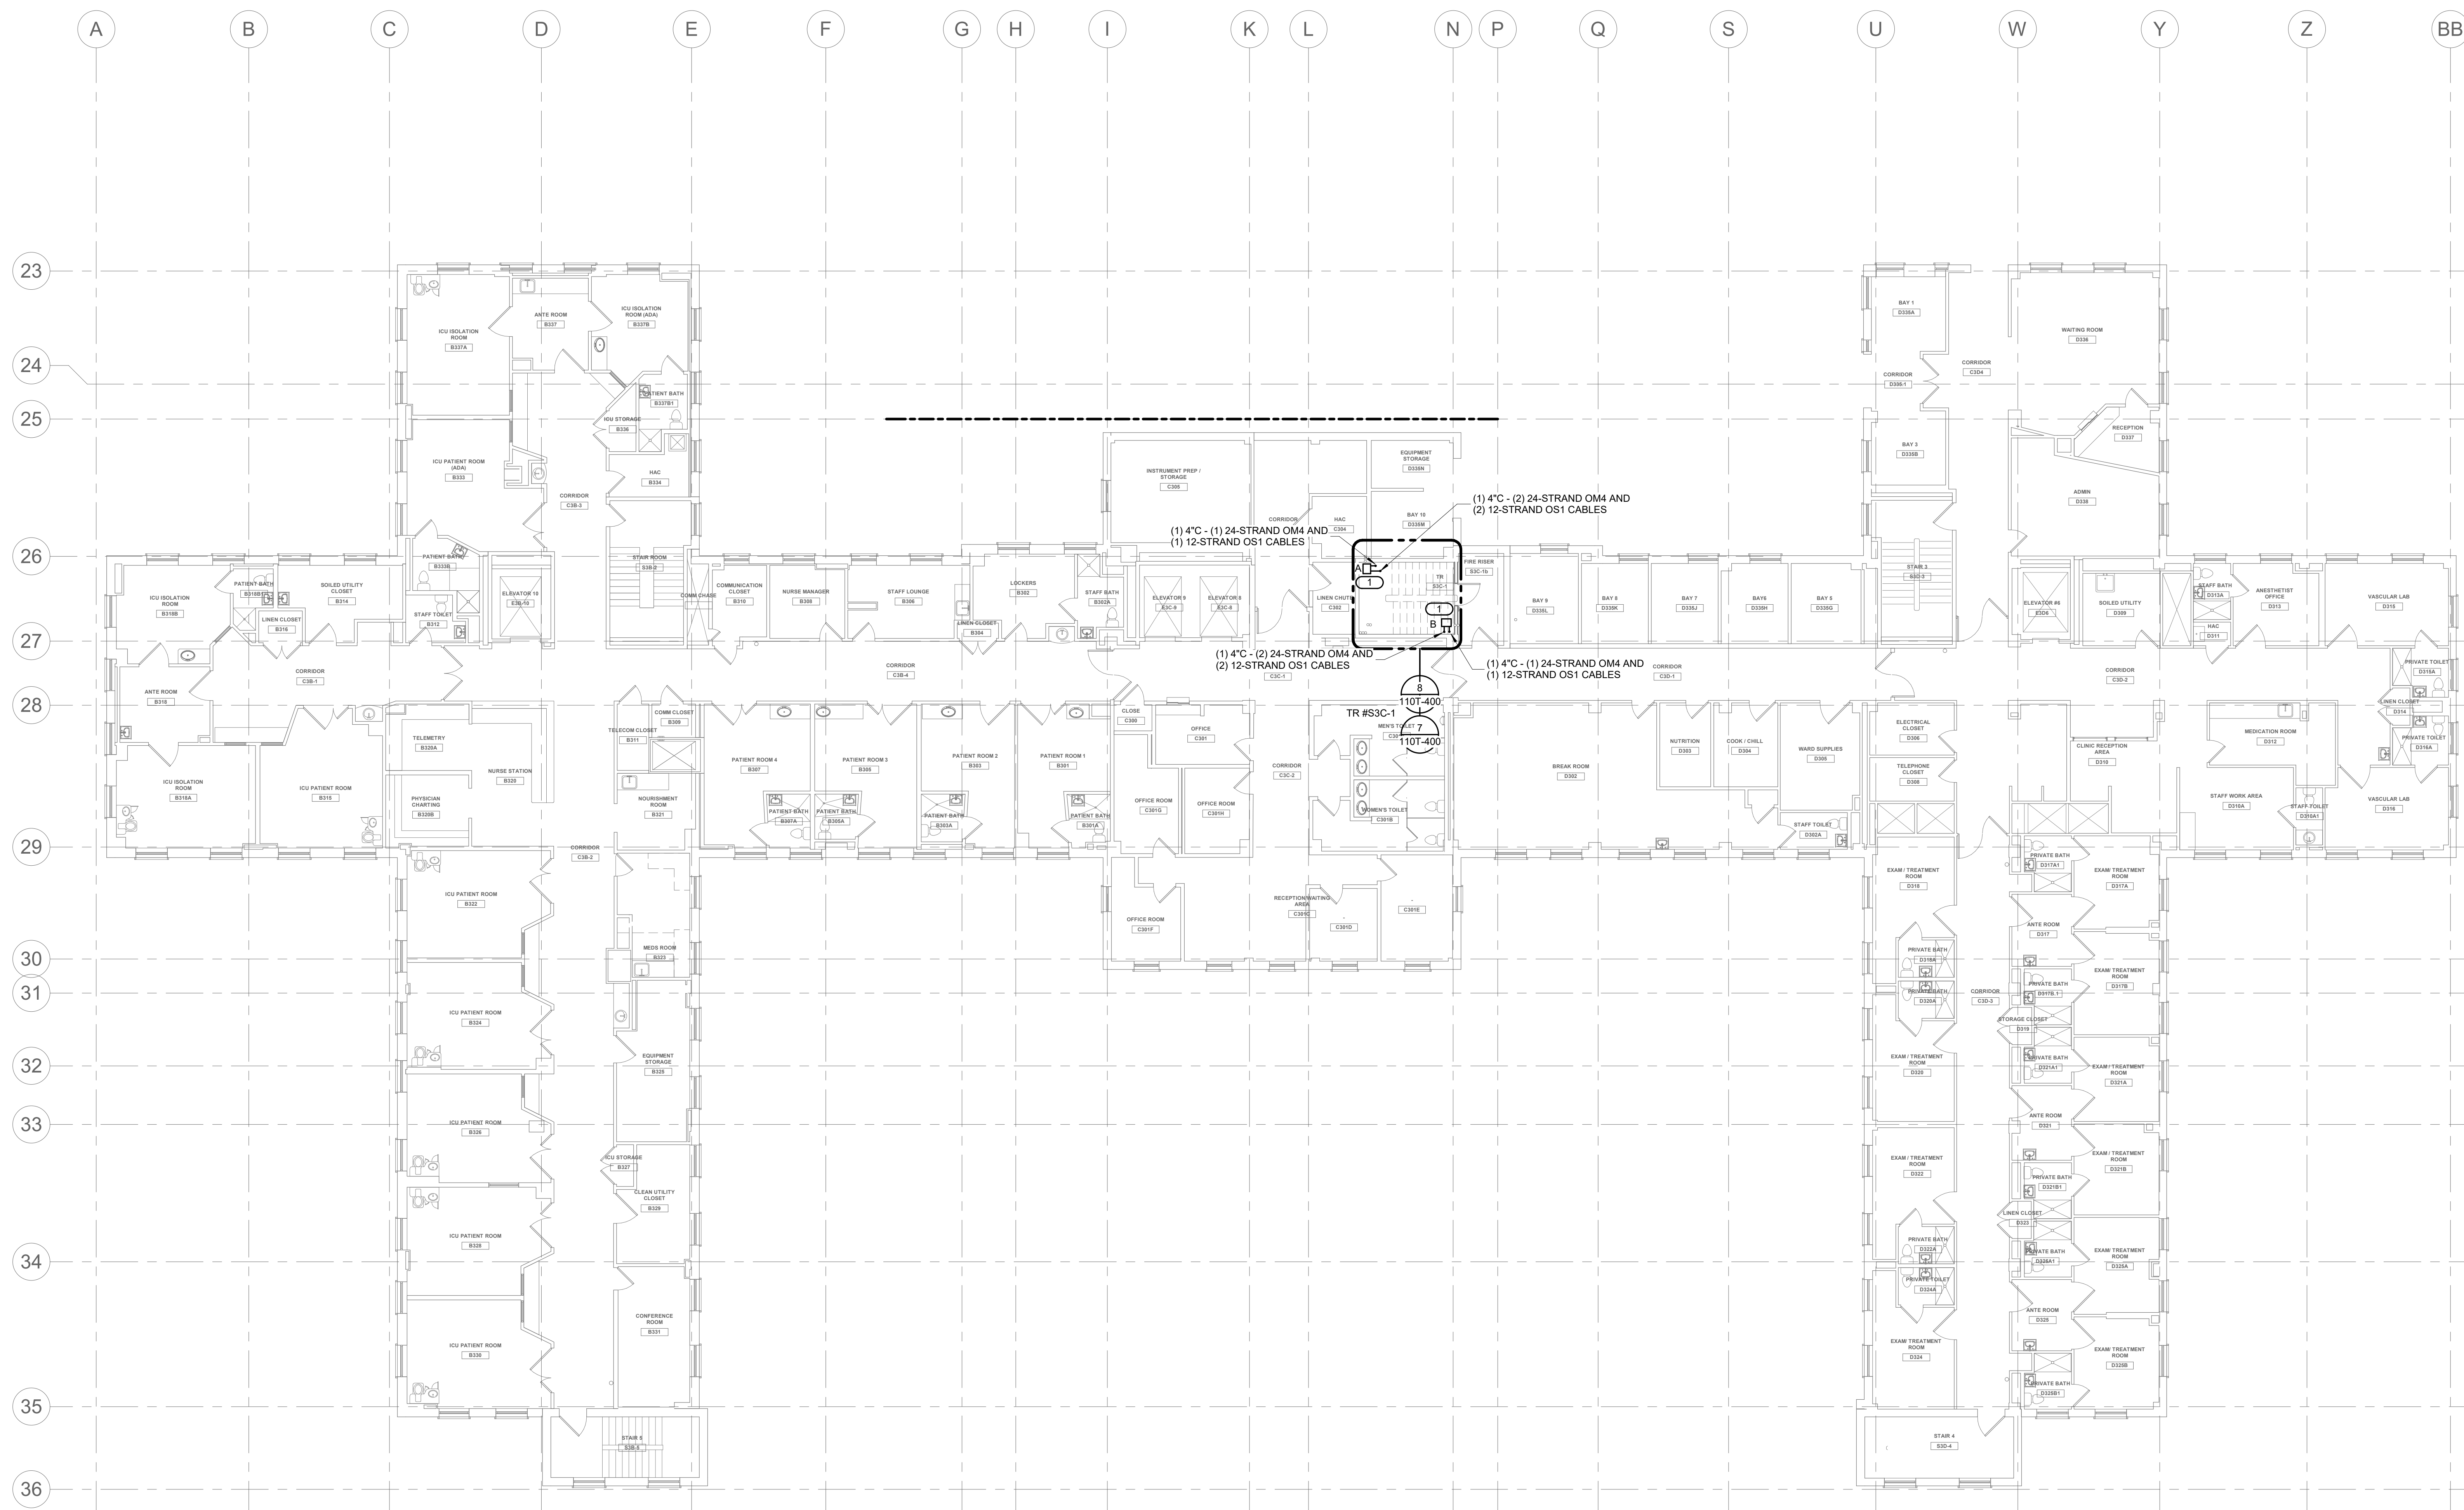

		CONSULTANT ENGINEERING DISCIPLINE:  www.imegcorp.com 225 W WASHINGTON STREET SUITE 2700 CHICAGO, IL 60608 P-312.294.0501 F-312.294.0003 PROJECT #22010109.00		ARCHITECT/ENGINEER OF RECORD A/E: SPEES DESIGN BUILD 23830 PACIFIC HIGHWAY S. SUITE 203 KENT, WA 98032  SPEESDESIGNBUILD		STAMP  RCDD 		Office of Construction and Facilities Management VA U.S. Department of Veterans Affairs		Drawing Title BLDG.1110 LEVEL 03 PLAN - TECHNOLOGY		Phase 100% CONSTRUCTION DOCUMENTS		Project Title EHRM INFRASTRUCTURE UPGRADES - HAMPTON		Project Number 509-22-700 Building Number 110		Drawing Number 110T-203 678 of 713	
Revisions:		Date:						Approved:		FULLY SPRINKLERED		Location HAMPTON VA MEDICAL CENTER, HAMPTON, VIRGINIA		Issue Date 05/09/2025		Checked EW		Drawn IMEG	

SHEET NOTES:
1. REFER TO ENLARGED PLANS FOR ADDITIONAL INFORMATION.


KEY NOTES: (#)
1. ROUTE CONDUIT UP TO HEIGHT ABOVE CABLE TRAY. PROVIDE PULLBOX AND PENETRATION THRU CEILING TO ROUTE CONDUIT UP INTO TR #D502A.

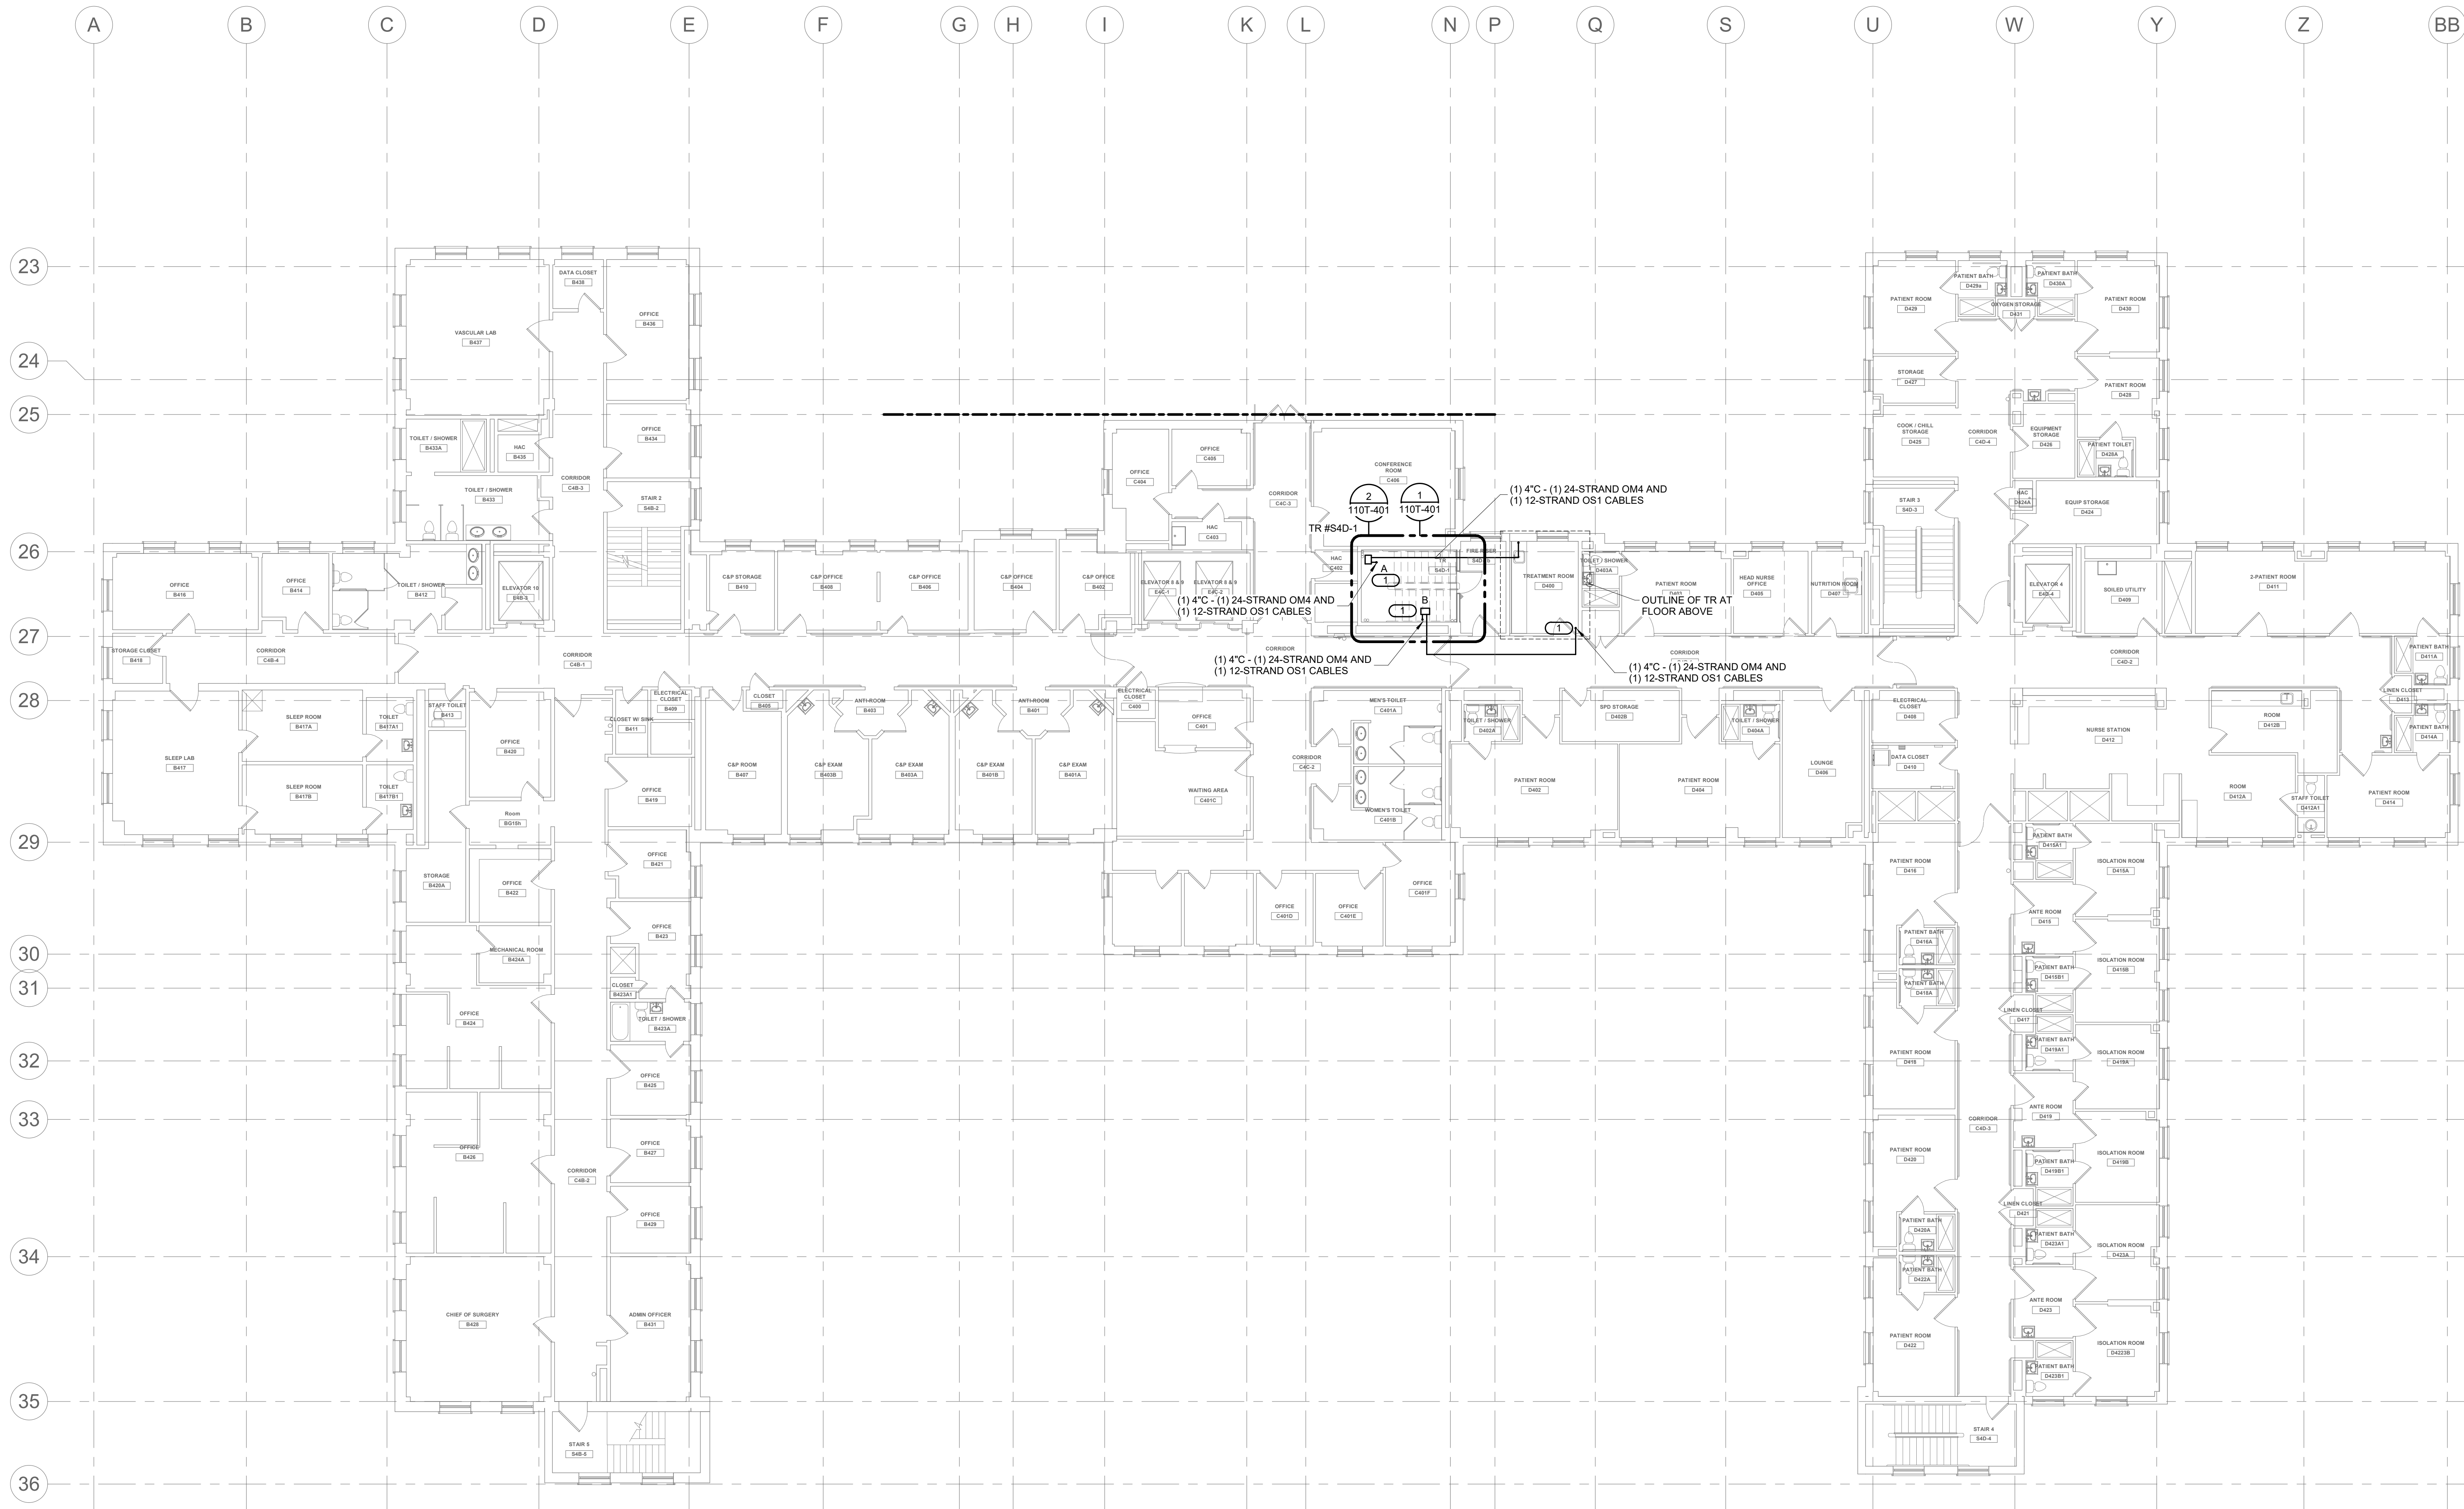

1 LEVEL 04 PLAN - TECHNOLOGY
1" = 10'-0"

Revisions:	
-----------------------	--	--	

- SHEET NOTES:**
1. REFER TO ENLARGED PLANS FOR ADDITIONAL INFORMATION.
- KEY NOTES:** (#)
1. ROUTE CONDUIT UP TO HEIGHT ABOVE CABLE TRAY.
2. TR #0502A SHALL SERVE NETWORK DEVICES ON SIXTH FLOOR OF BLDG 110.

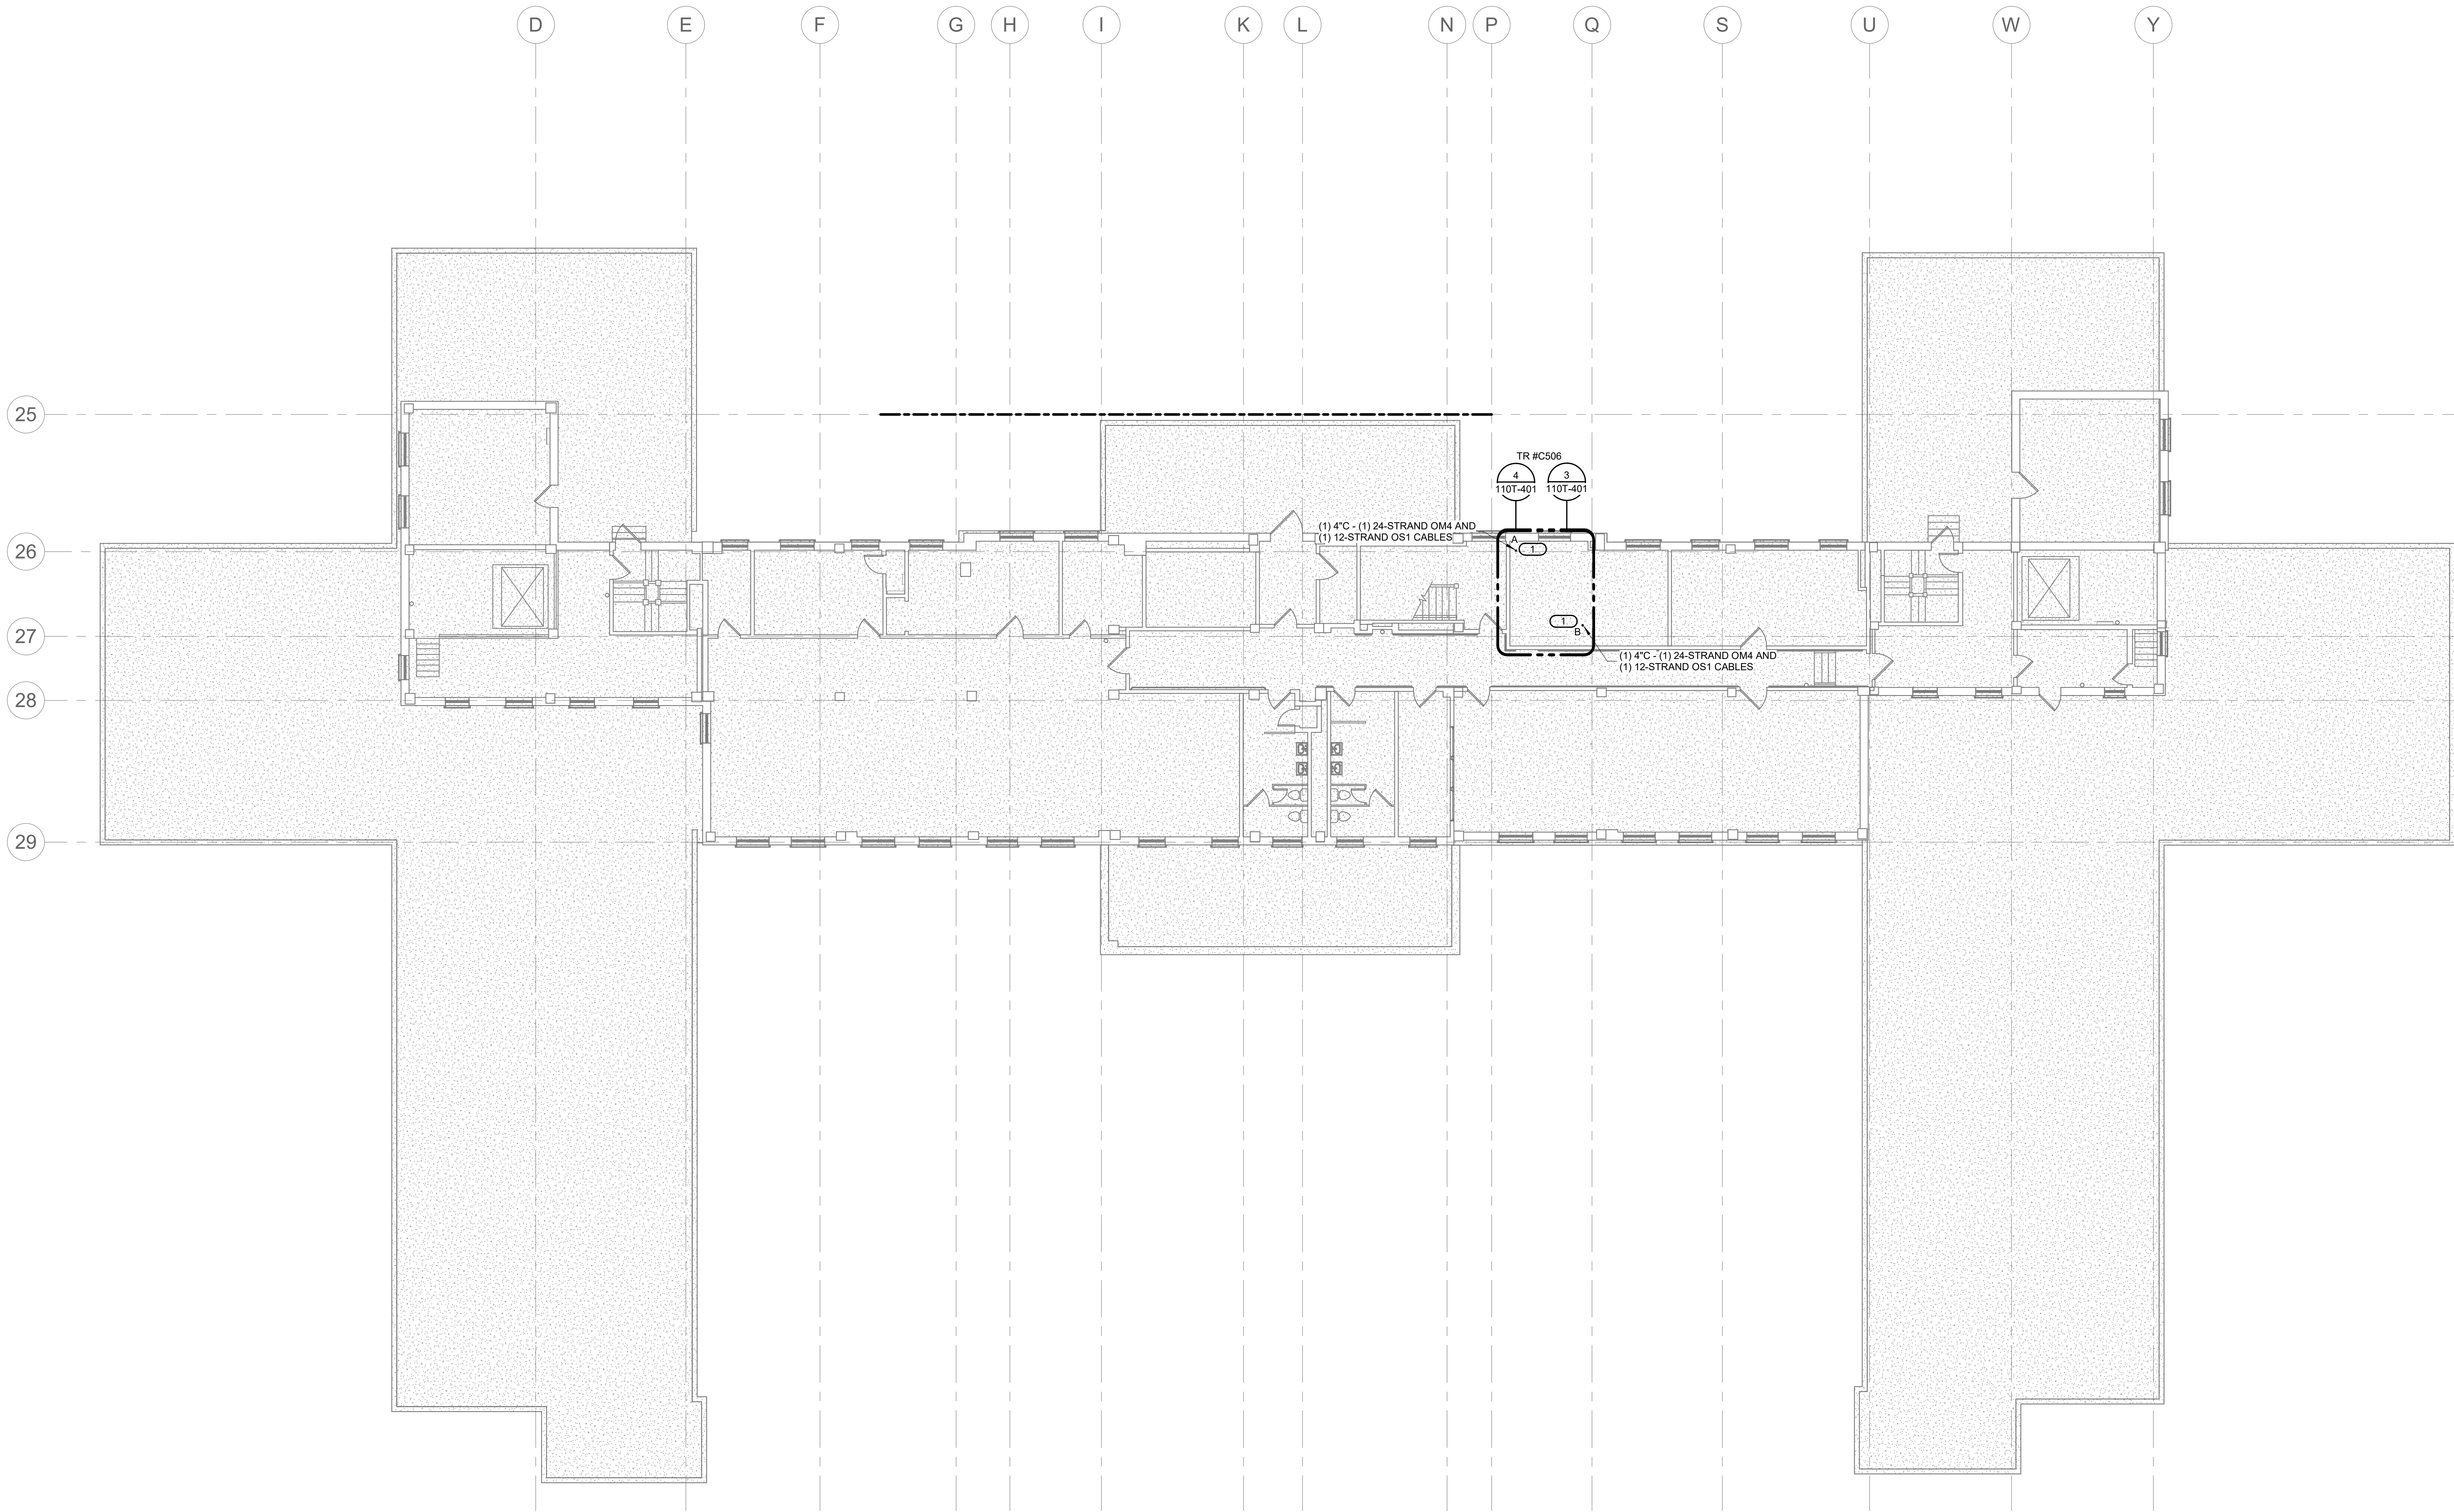

1 LEVEL 05 PLAN - TECHNOLOGY
1" = 10'-0"

Revisions:	Date:

CONSULTANT
ENGINEERING DISCIPLINE:
IMEG
225 W WASHINGTON STREET
SUITE 2700
CHICAGO, IL 60609
P: 312.294.0501 F: 312.294.0003
PROJECT #22010109.00

ARCHITECT/ENGINEER OF RECORD
A/E:
SPEES DESIGN BUILD
23830 PACIFIC HIGHWAY S. SUITE 203
KENT, WA 98032
SDB SPEESDESIGNBUILD

STAMP
Bicsi
REGISTERED COMMUNICATIONS DISTRIBUTION DESIGNER
REG. NO. 1519026
EXPIRES 03/31/2025
RCDD

Office of
Construction
and Facilities
Management
VA U.S. Department
of Veterans Affairs

Drawing Title BLDG.110 LEVEL 05 PLAN - TECHNOLOGY
Approved:

Phase 100% CONSTRUCTION DOCUMENTS
FULLY SPRINKLERED

Project Title EHRM INFRASTRUCTURE UPGRADES - HAMPTON
Location HAMPTON VA MEDICAL CENTER, HAMPTON, VIRGINIA
Issue Date 05/09/2025
Checked EW
Drawn IMEG

Project Number 509-22-700
Building Number 110
Drawing Number 110T-205
680 of 713

A

B

C

D

E

F

A


B

C

D

E

F

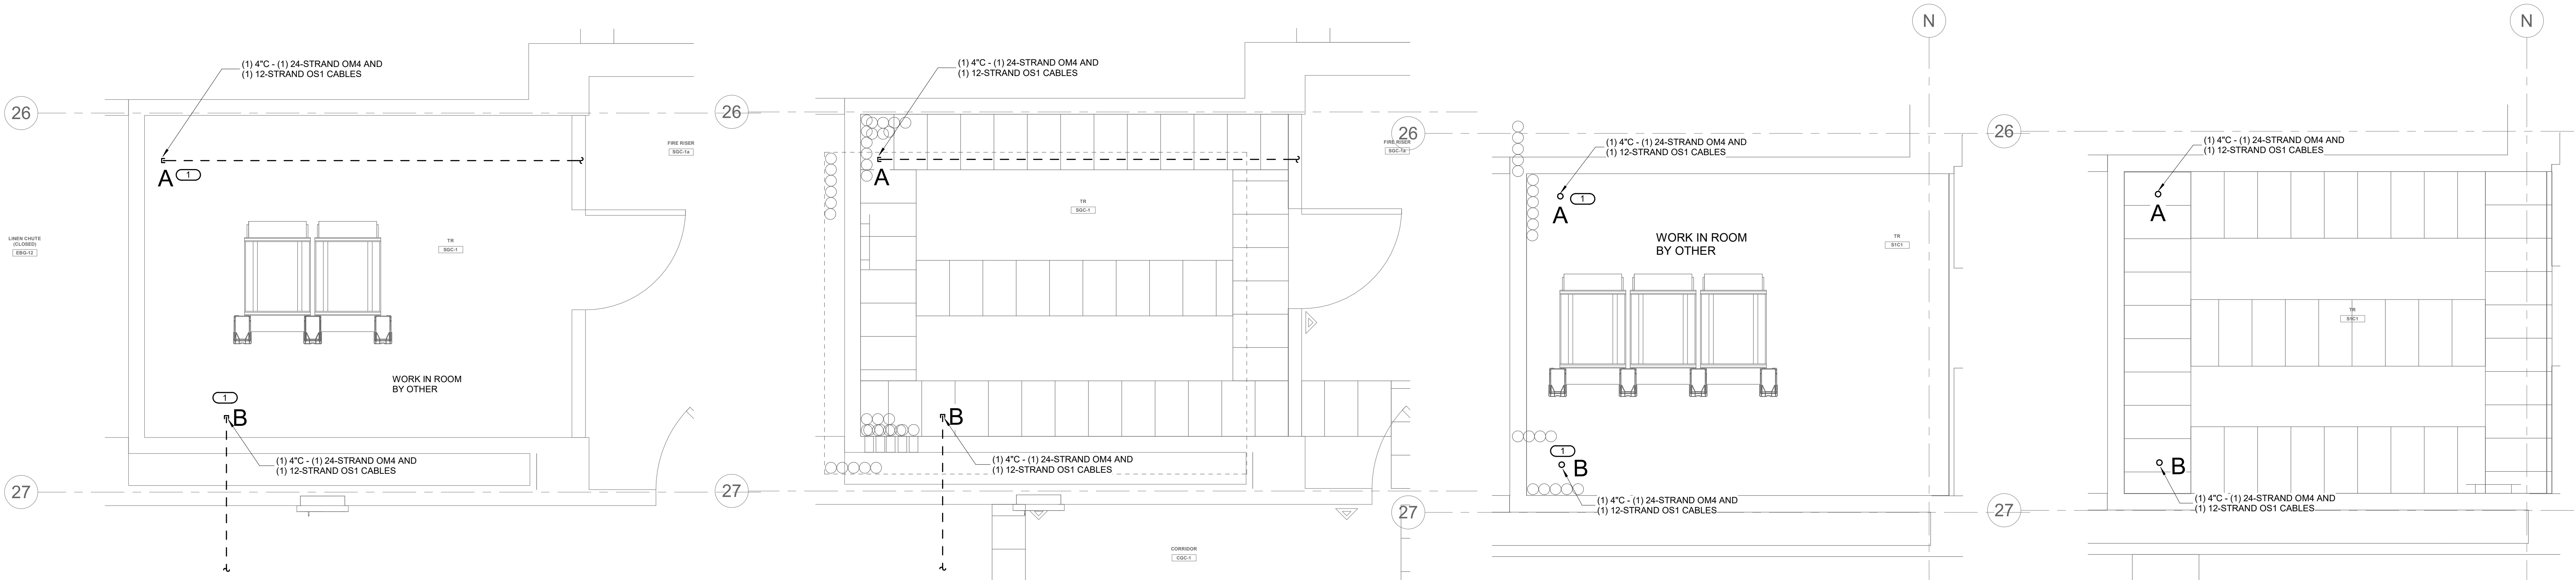

1 TELECOM ROOM ENLARGEMENT TR #SGC-1
1/2" = 1'-0"

NOTES:
1. REFER TO ELECTRICAL DRAWINGS FOR ROOM LAYOUT AND RACK ELEVATIONS.
2. ROUTE OPTICAL FIBER CABLE TO OVERHEAD CABLE TRAY AND TERMINATE IN FIBER DISTRIBUTION CABINET.

KEYNOTES: (1)
1. THROUGH WALL PENETRATION FOR BACKBONE CONDUIT. OPTICAL FIBER CABLE CONTINUES ON CABLE TRAY TO RACKS.


2 TELECOM ROOM PATHWAY TR #SGC-1
1/2" = 1'-0"

3 TELECOM ROOM ENLARGEMENT TR #S1C1
1/2" = 1'-0"

NOTES:
1. REFER TO ELECTRICAL DRAWINGS FOR ROOM LAYOUT AND RACK ELEVATIONS.
2. ROUTE OPTICAL FIBER CABLE TO OVERHEAD CABLE TRAY AND TERMINATE IN FIBER DISTRIBUTION CABINET.

KEYNOTES: (1)
1. THROUGH WALL PENETRATION FOR BACKBONE CONDUIT. OPTICAL FIBER CABLE CONTINUES ON CABLE TRAY TO RACKS.

4 TELECOM ROOM PATHWAY TR #S1C1
1/2" = 1'-0"

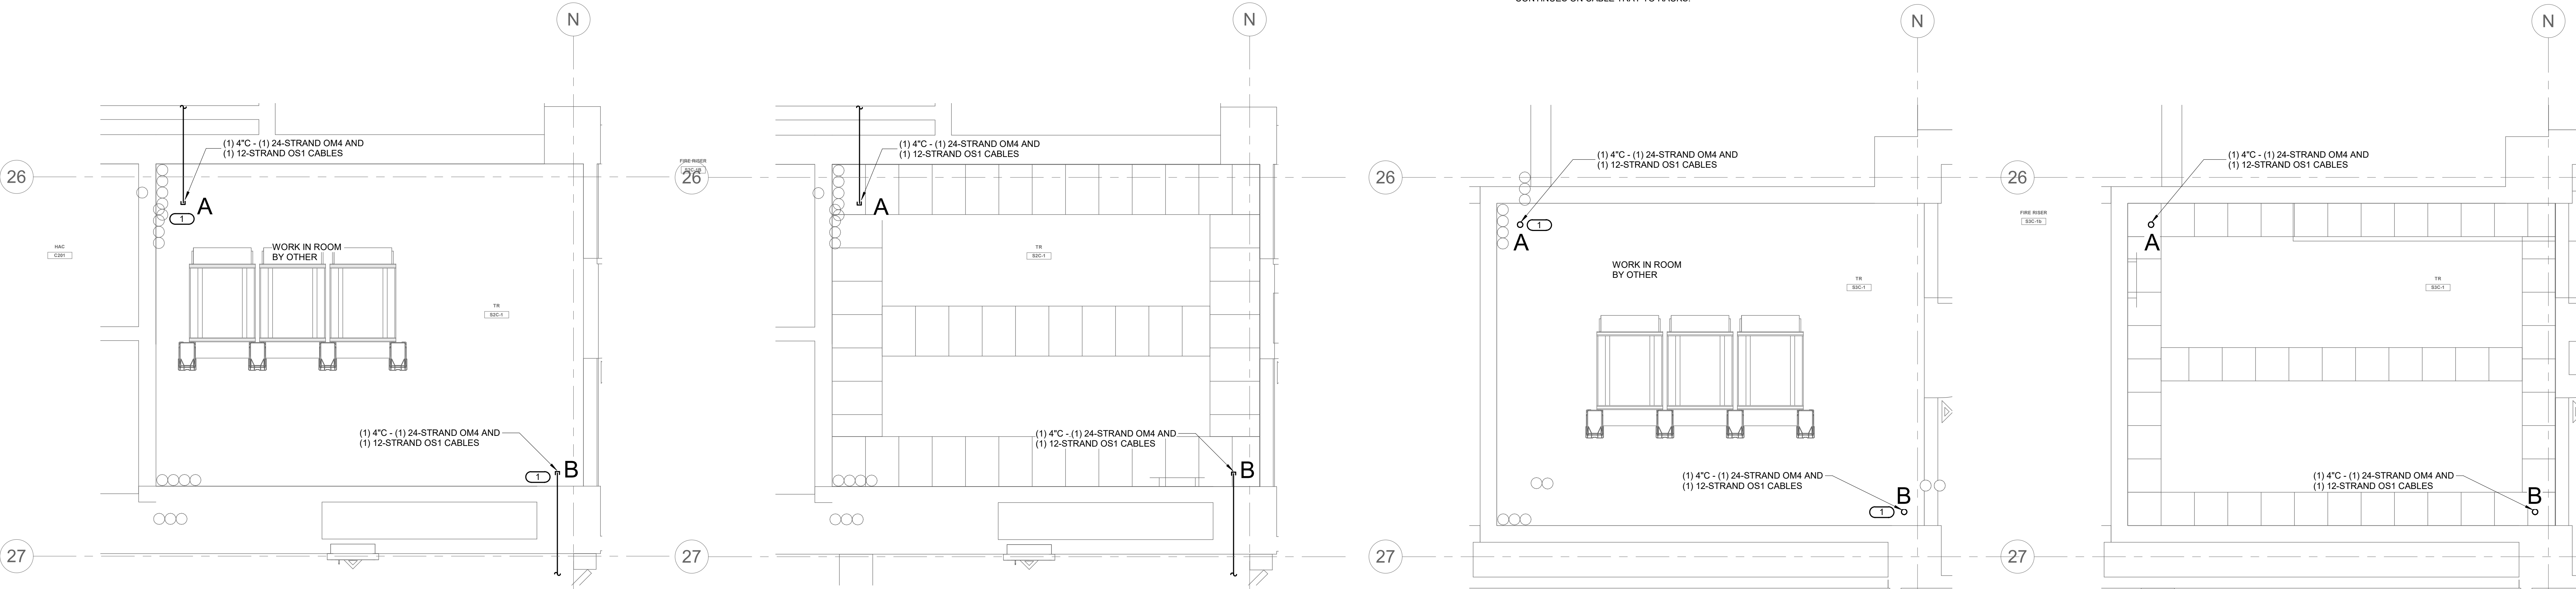

5 TELECOM ROOM ENLARGEMENT TR- #S2C-1
1/2" = 1'-0"

NOTES:
1. REFER TO ELECTRICAL DRAWINGS FOR ROOM LAYOUT AND RACK ELEVATIONS.
2. ROUTE OPTICAL FIBER CABLE TO OVERHEAD CABLE TRAY AND TERMINATE IN FIBER DISTRIBUTION CABINET.

KEYNOTES: (1)
1. THROUGH WALL PENETRATION FOR BACKBONE CONDUIT. OPTICAL FIBER CABLE CONTINUES ON CABLE TRAY TO RACKS.

6 TELECOM ROOM PATHWAY TR #S2C-1
1/2" = 1'-0"



7 TELECOM ROOM ENLARGEMENT TR #S3C-1
1/2" = 1'-0"

NOTES:
1. REFER TO ELECTRICAL DRAWINGS FOR ROOM LAYOUT AND RACK ELEVATIONS.
2. ROUTE OPTICAL FIBER CABLE TO OVERHEAD CABLE TRAY AND TERMINATE IN FIBER DISTRIBUTION CABINET.

KEYNOTES: (1)
1. THROUGH WALL PENETRATION FOR BACKBONE CONDUIT. OPTICAL FIBER CABLE CONTINUES ON CABLE TRAY TO RACKS.

8 TELECOM ROOM PATHWAY TR #S3C-1
1/2" = 1'-0"

--	--	

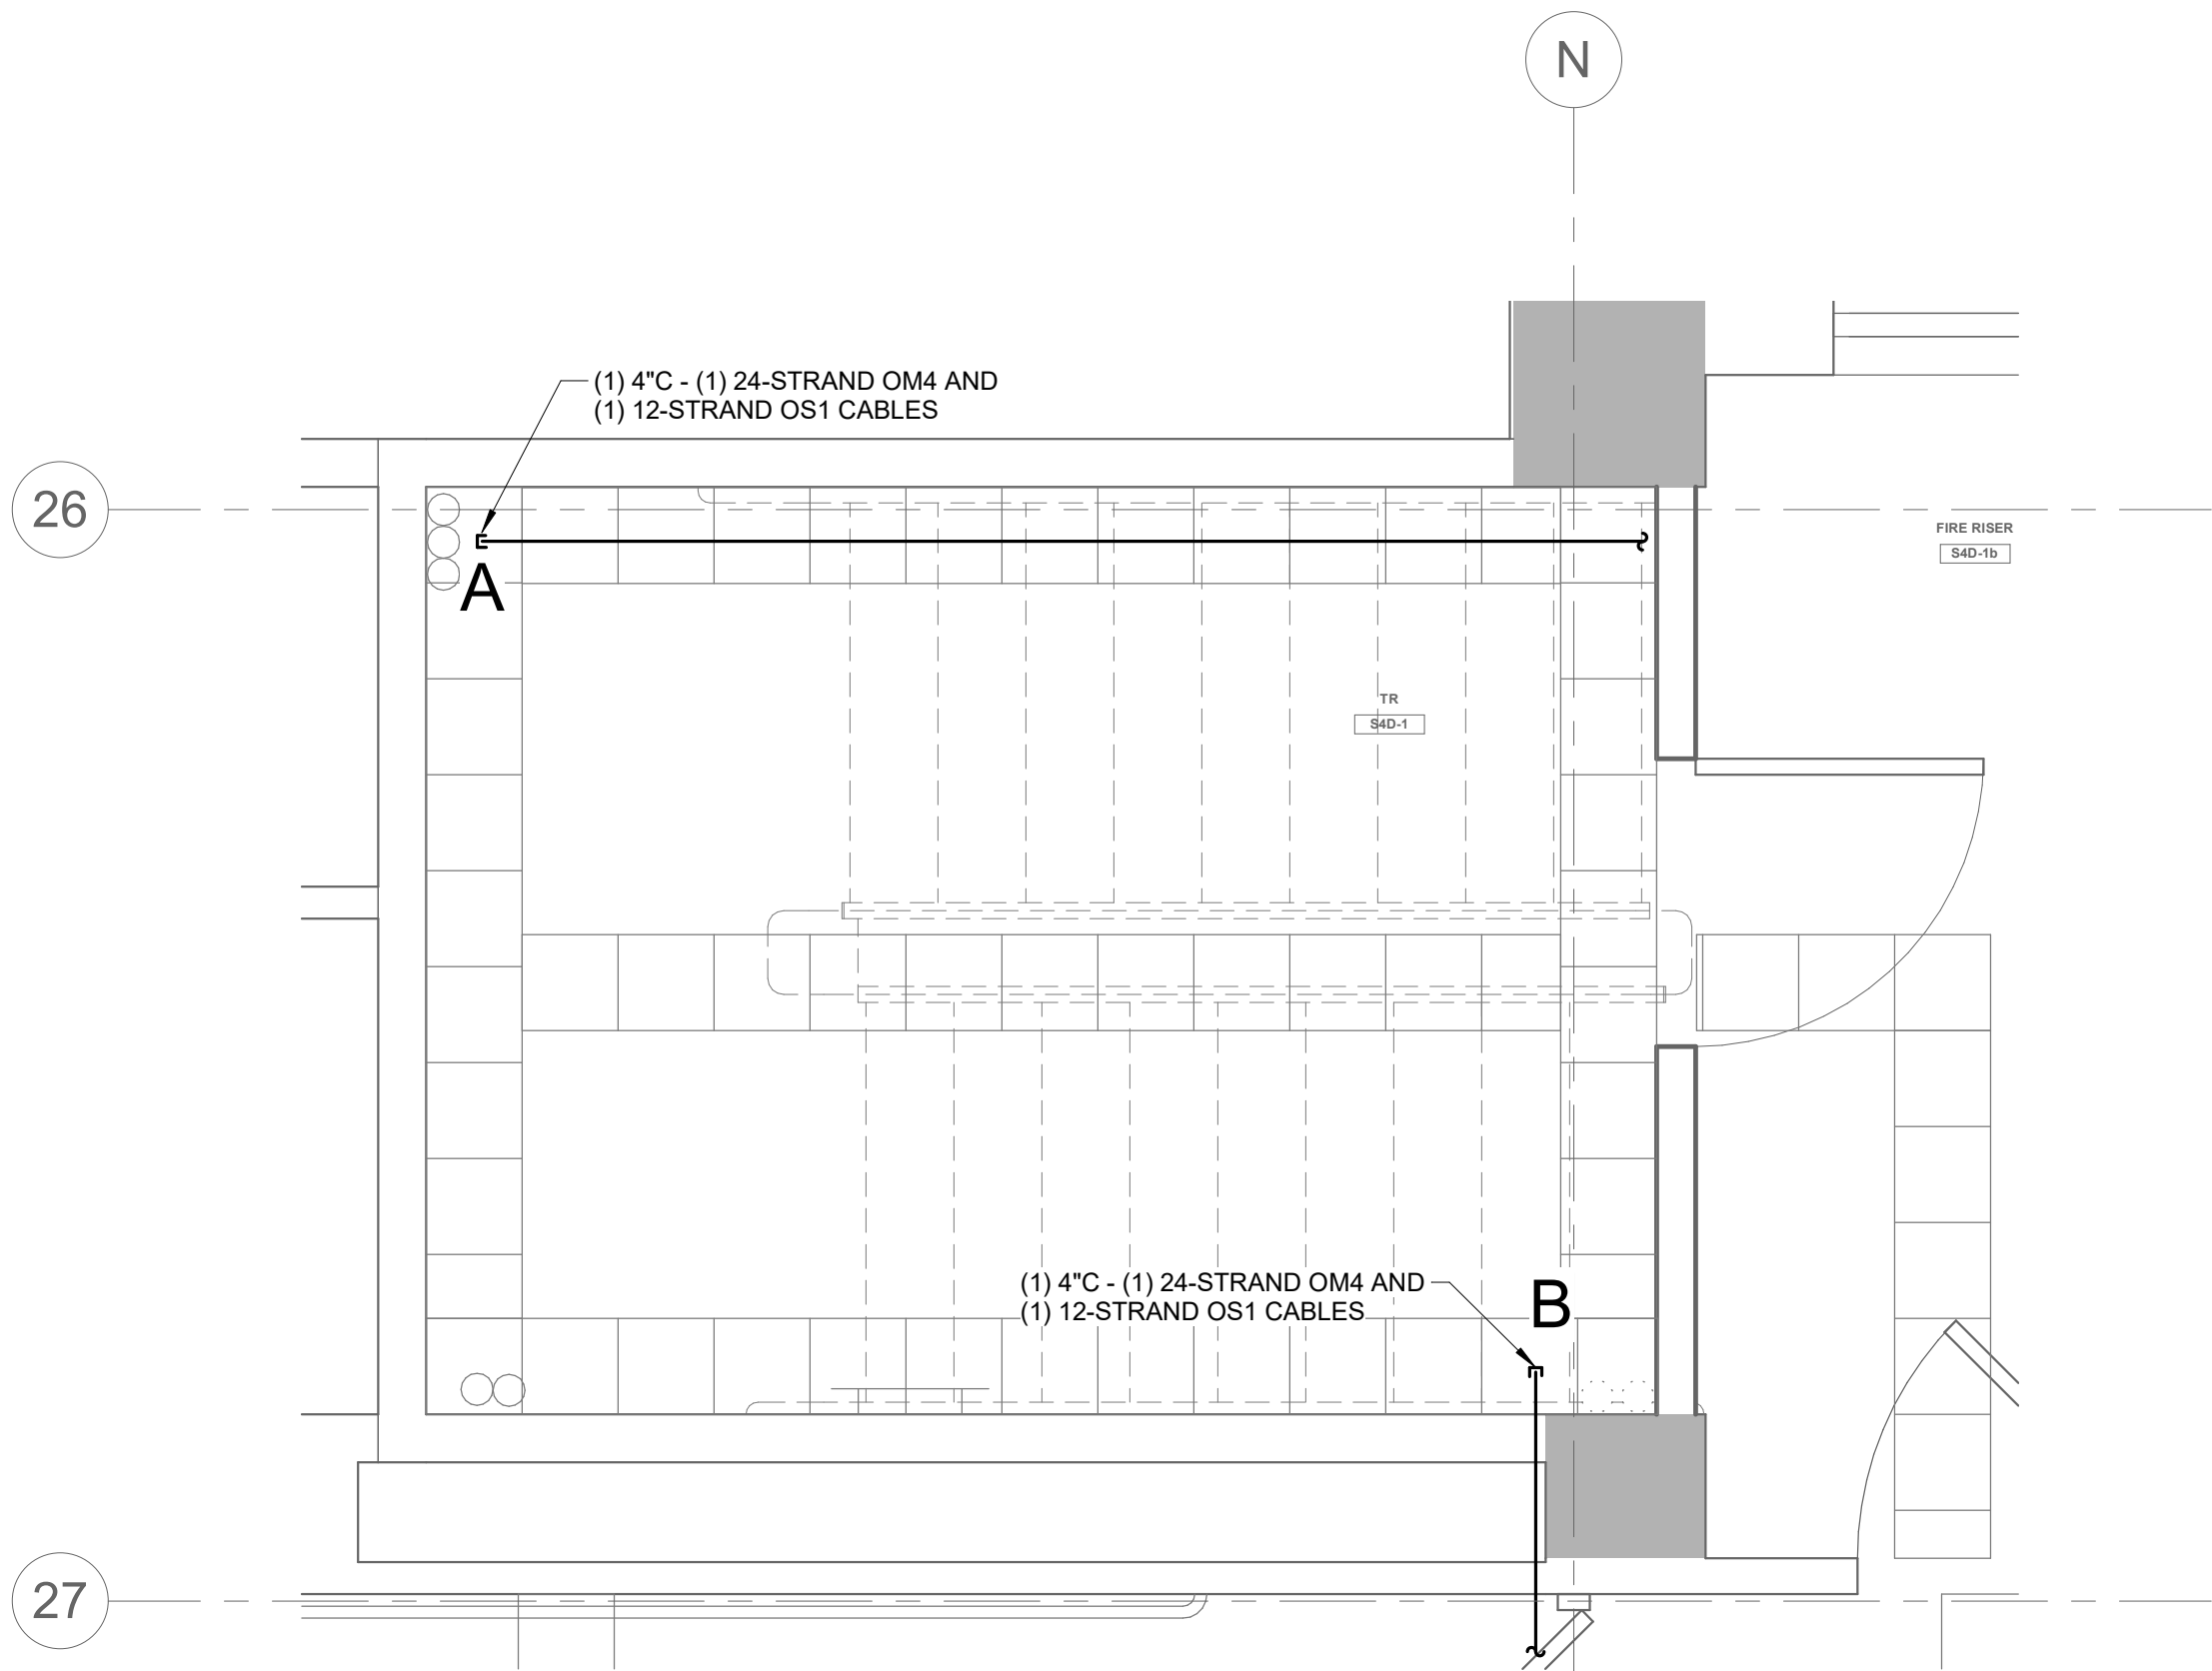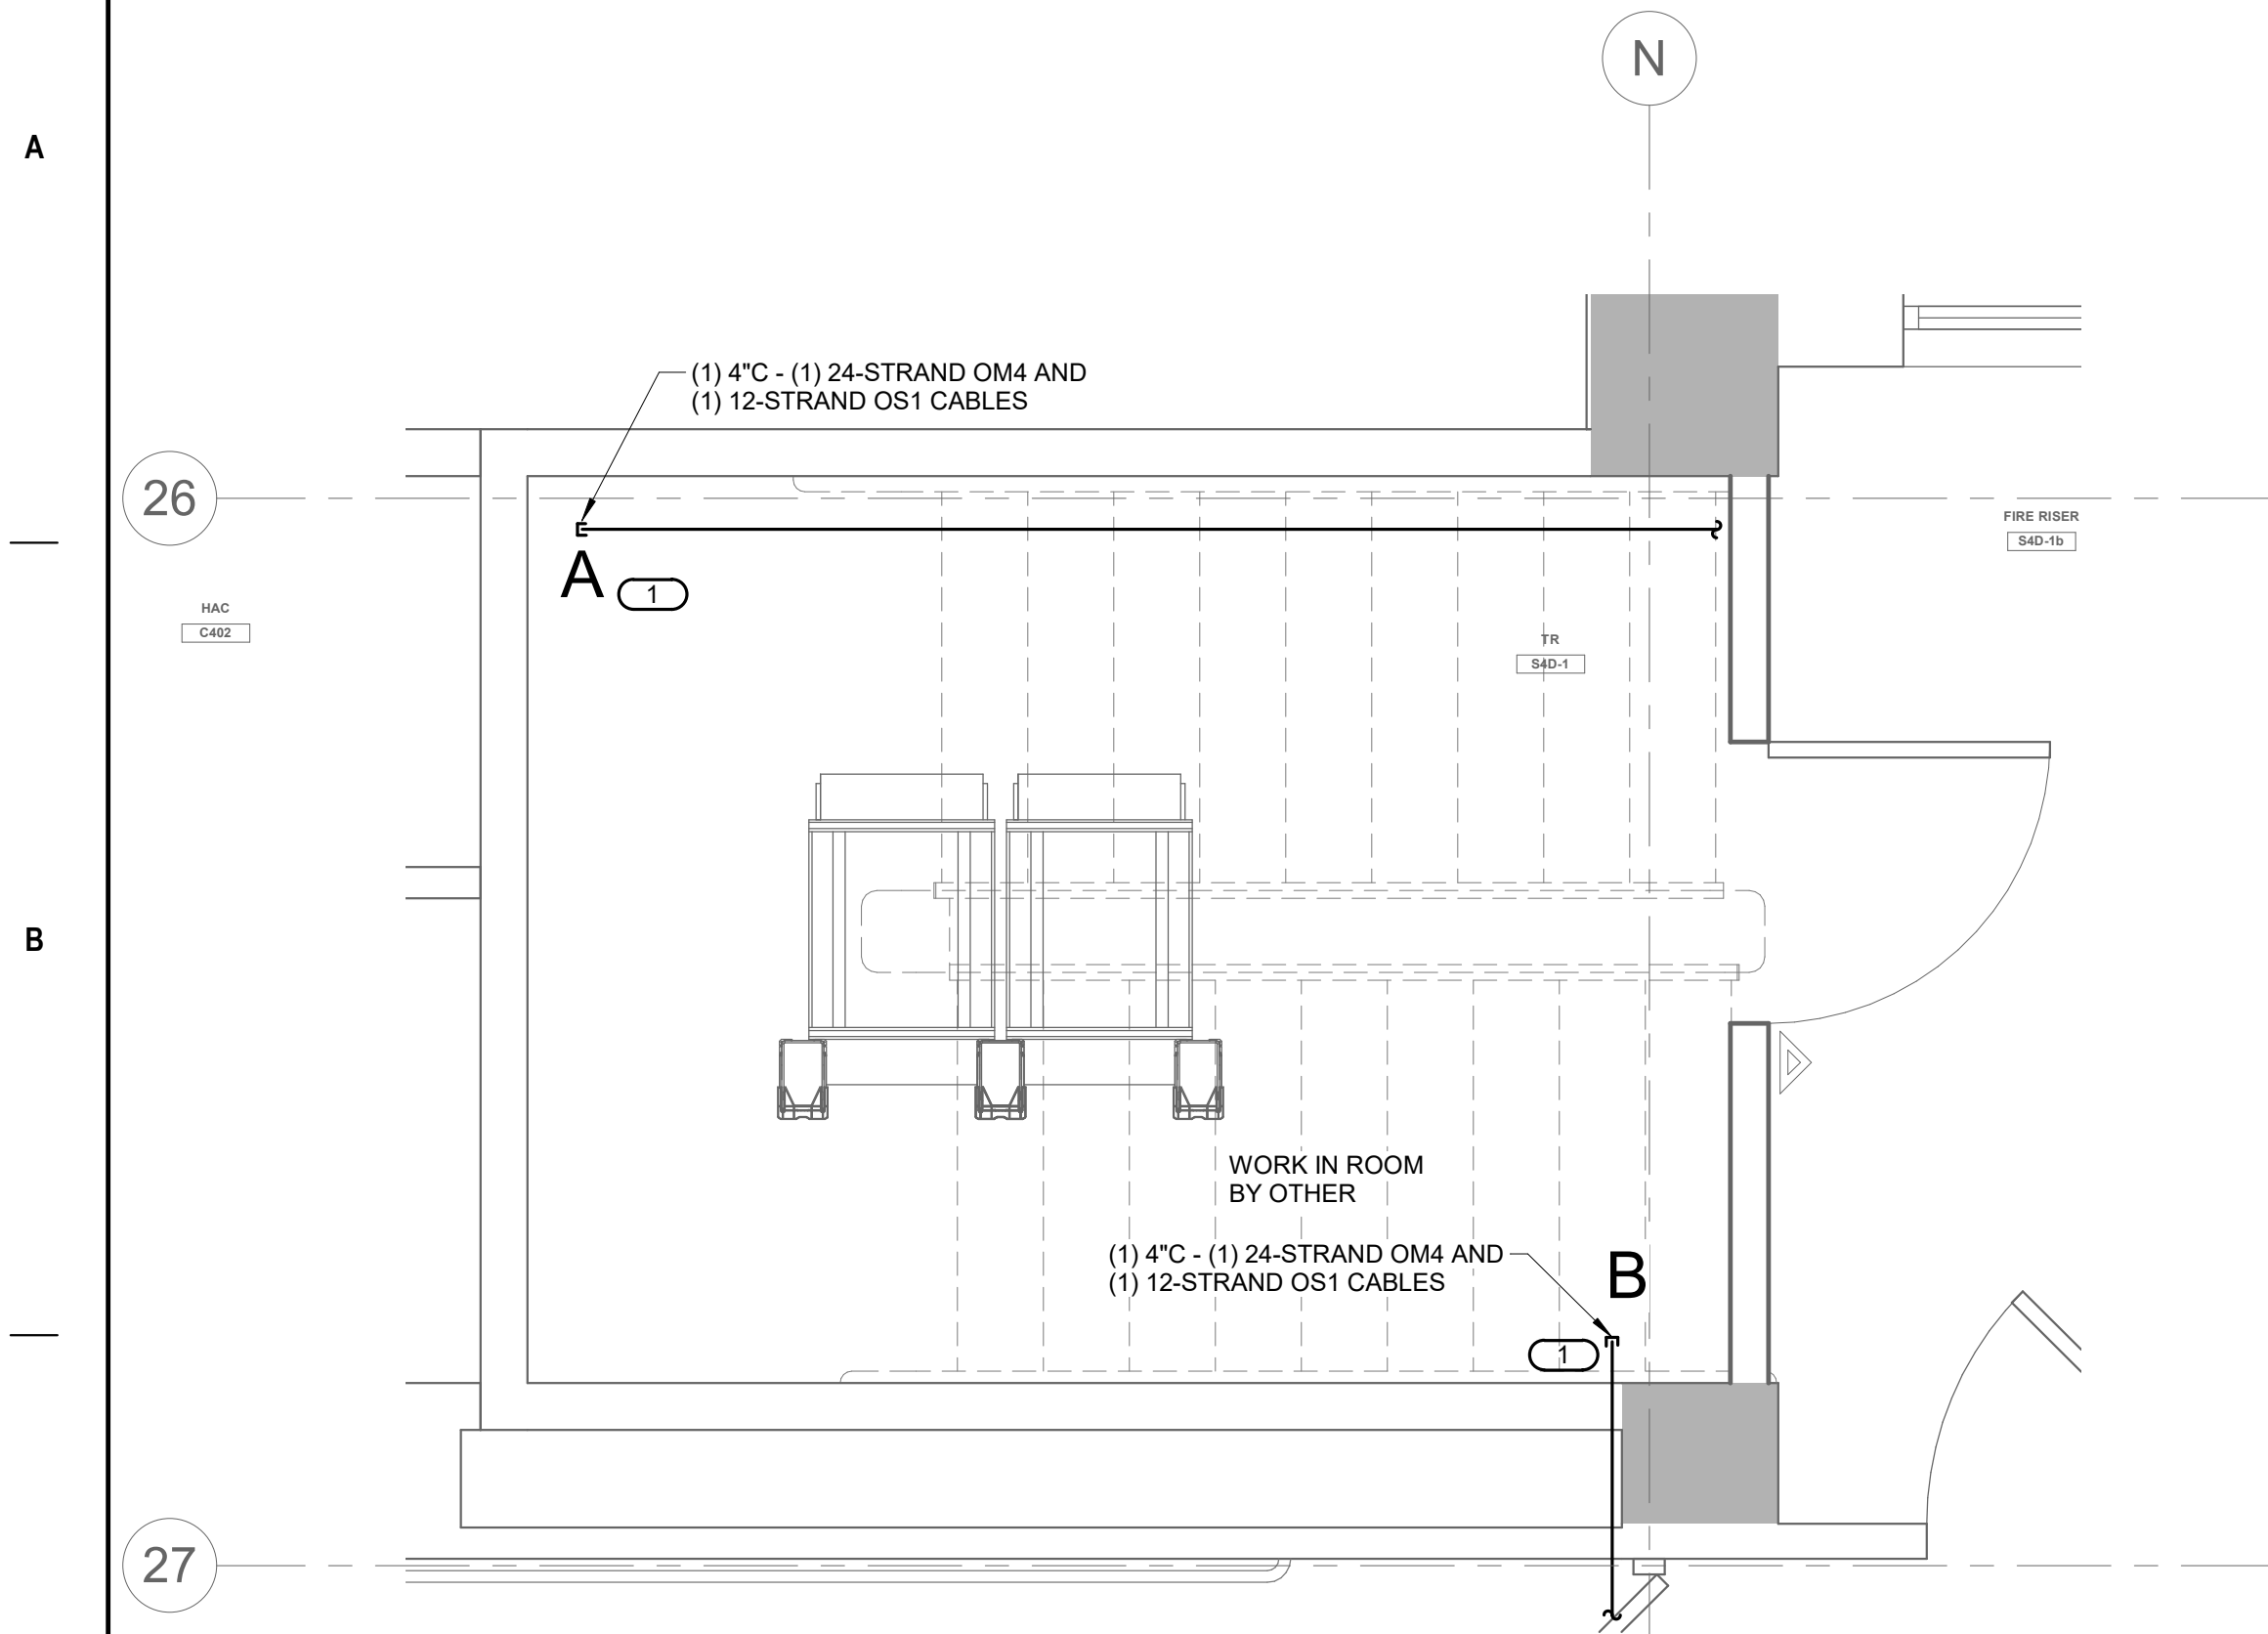

NORTH

1

1/2" = 1'-0"

TELECOM ENLARGEMENT TR #S4D-1

NOTES:

1. REFER TO ELECTRICAL DRAWINGS FOR ROOM LAYOUT AND RACK ELEVATIONS.

2. ROUTE OPTICAL FIBER CABLE TO OVERHEAD CABLE TRAY AND TERMINATE IN FIBER DISTRIBUTION CABINET.

KEYNOTES: **#**



1. THROUGH WALL PENETRATION FOR BACKBONE CONDUIT. OPTICAL FIBER CABLE CONTINUES ON CABLE TRAY TO RACKS.

NORTH

2

1/2" = 1'-0"

TELECOM ROOM PATHWAY TR #S4D-1

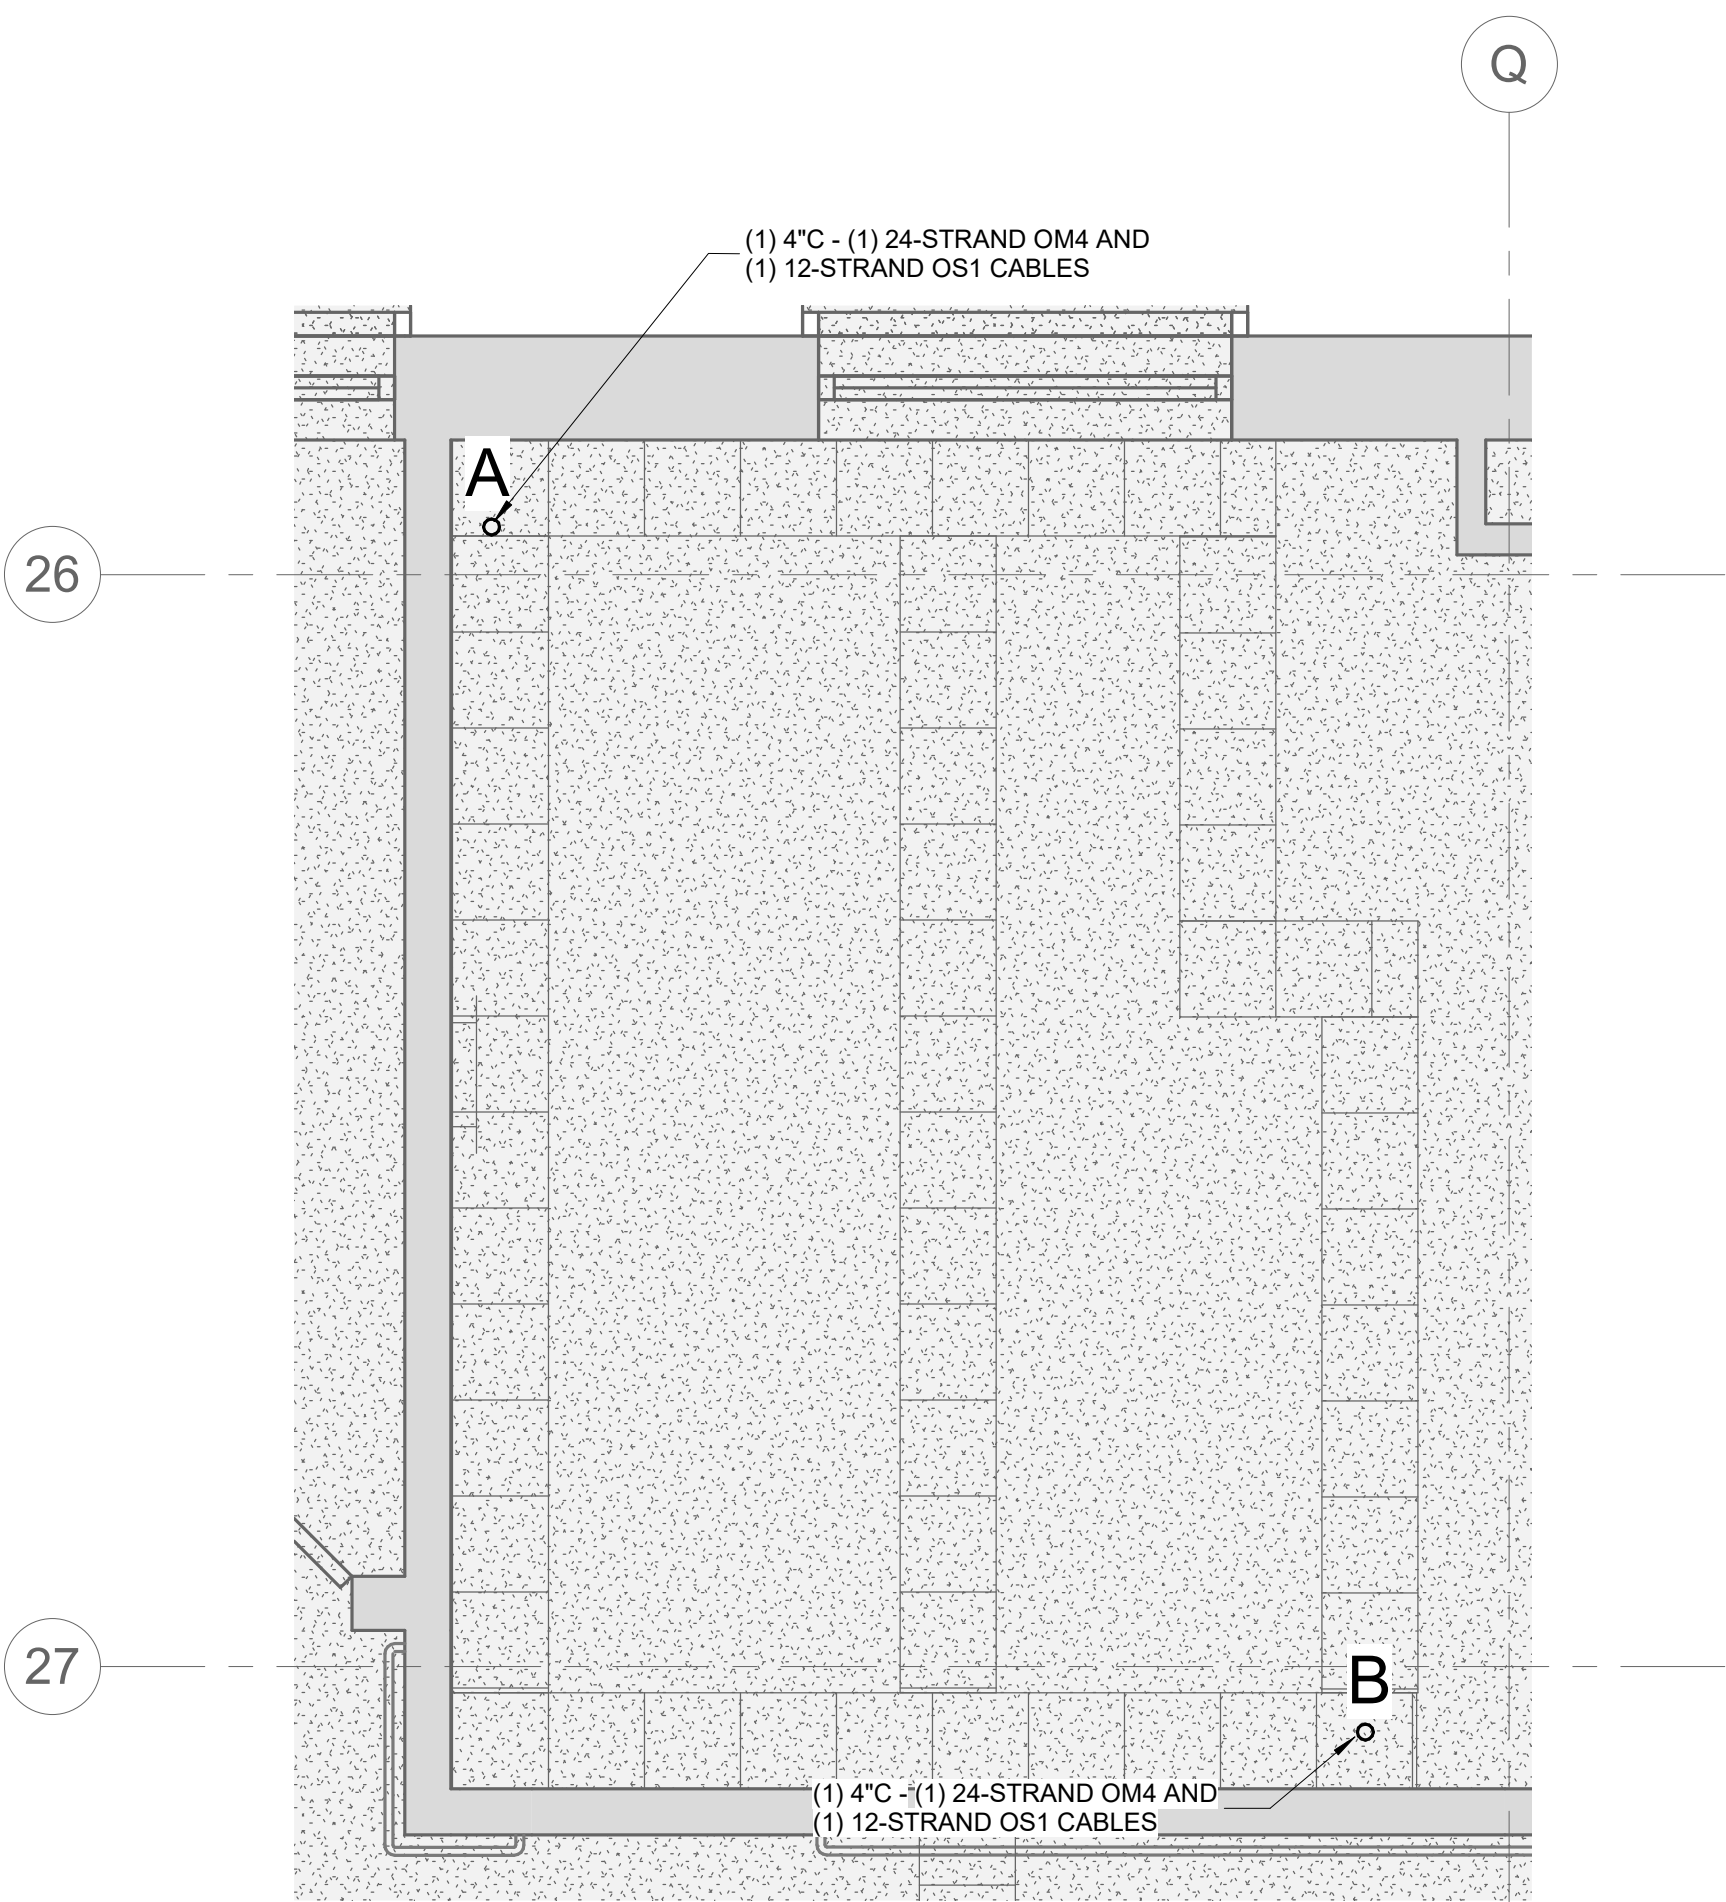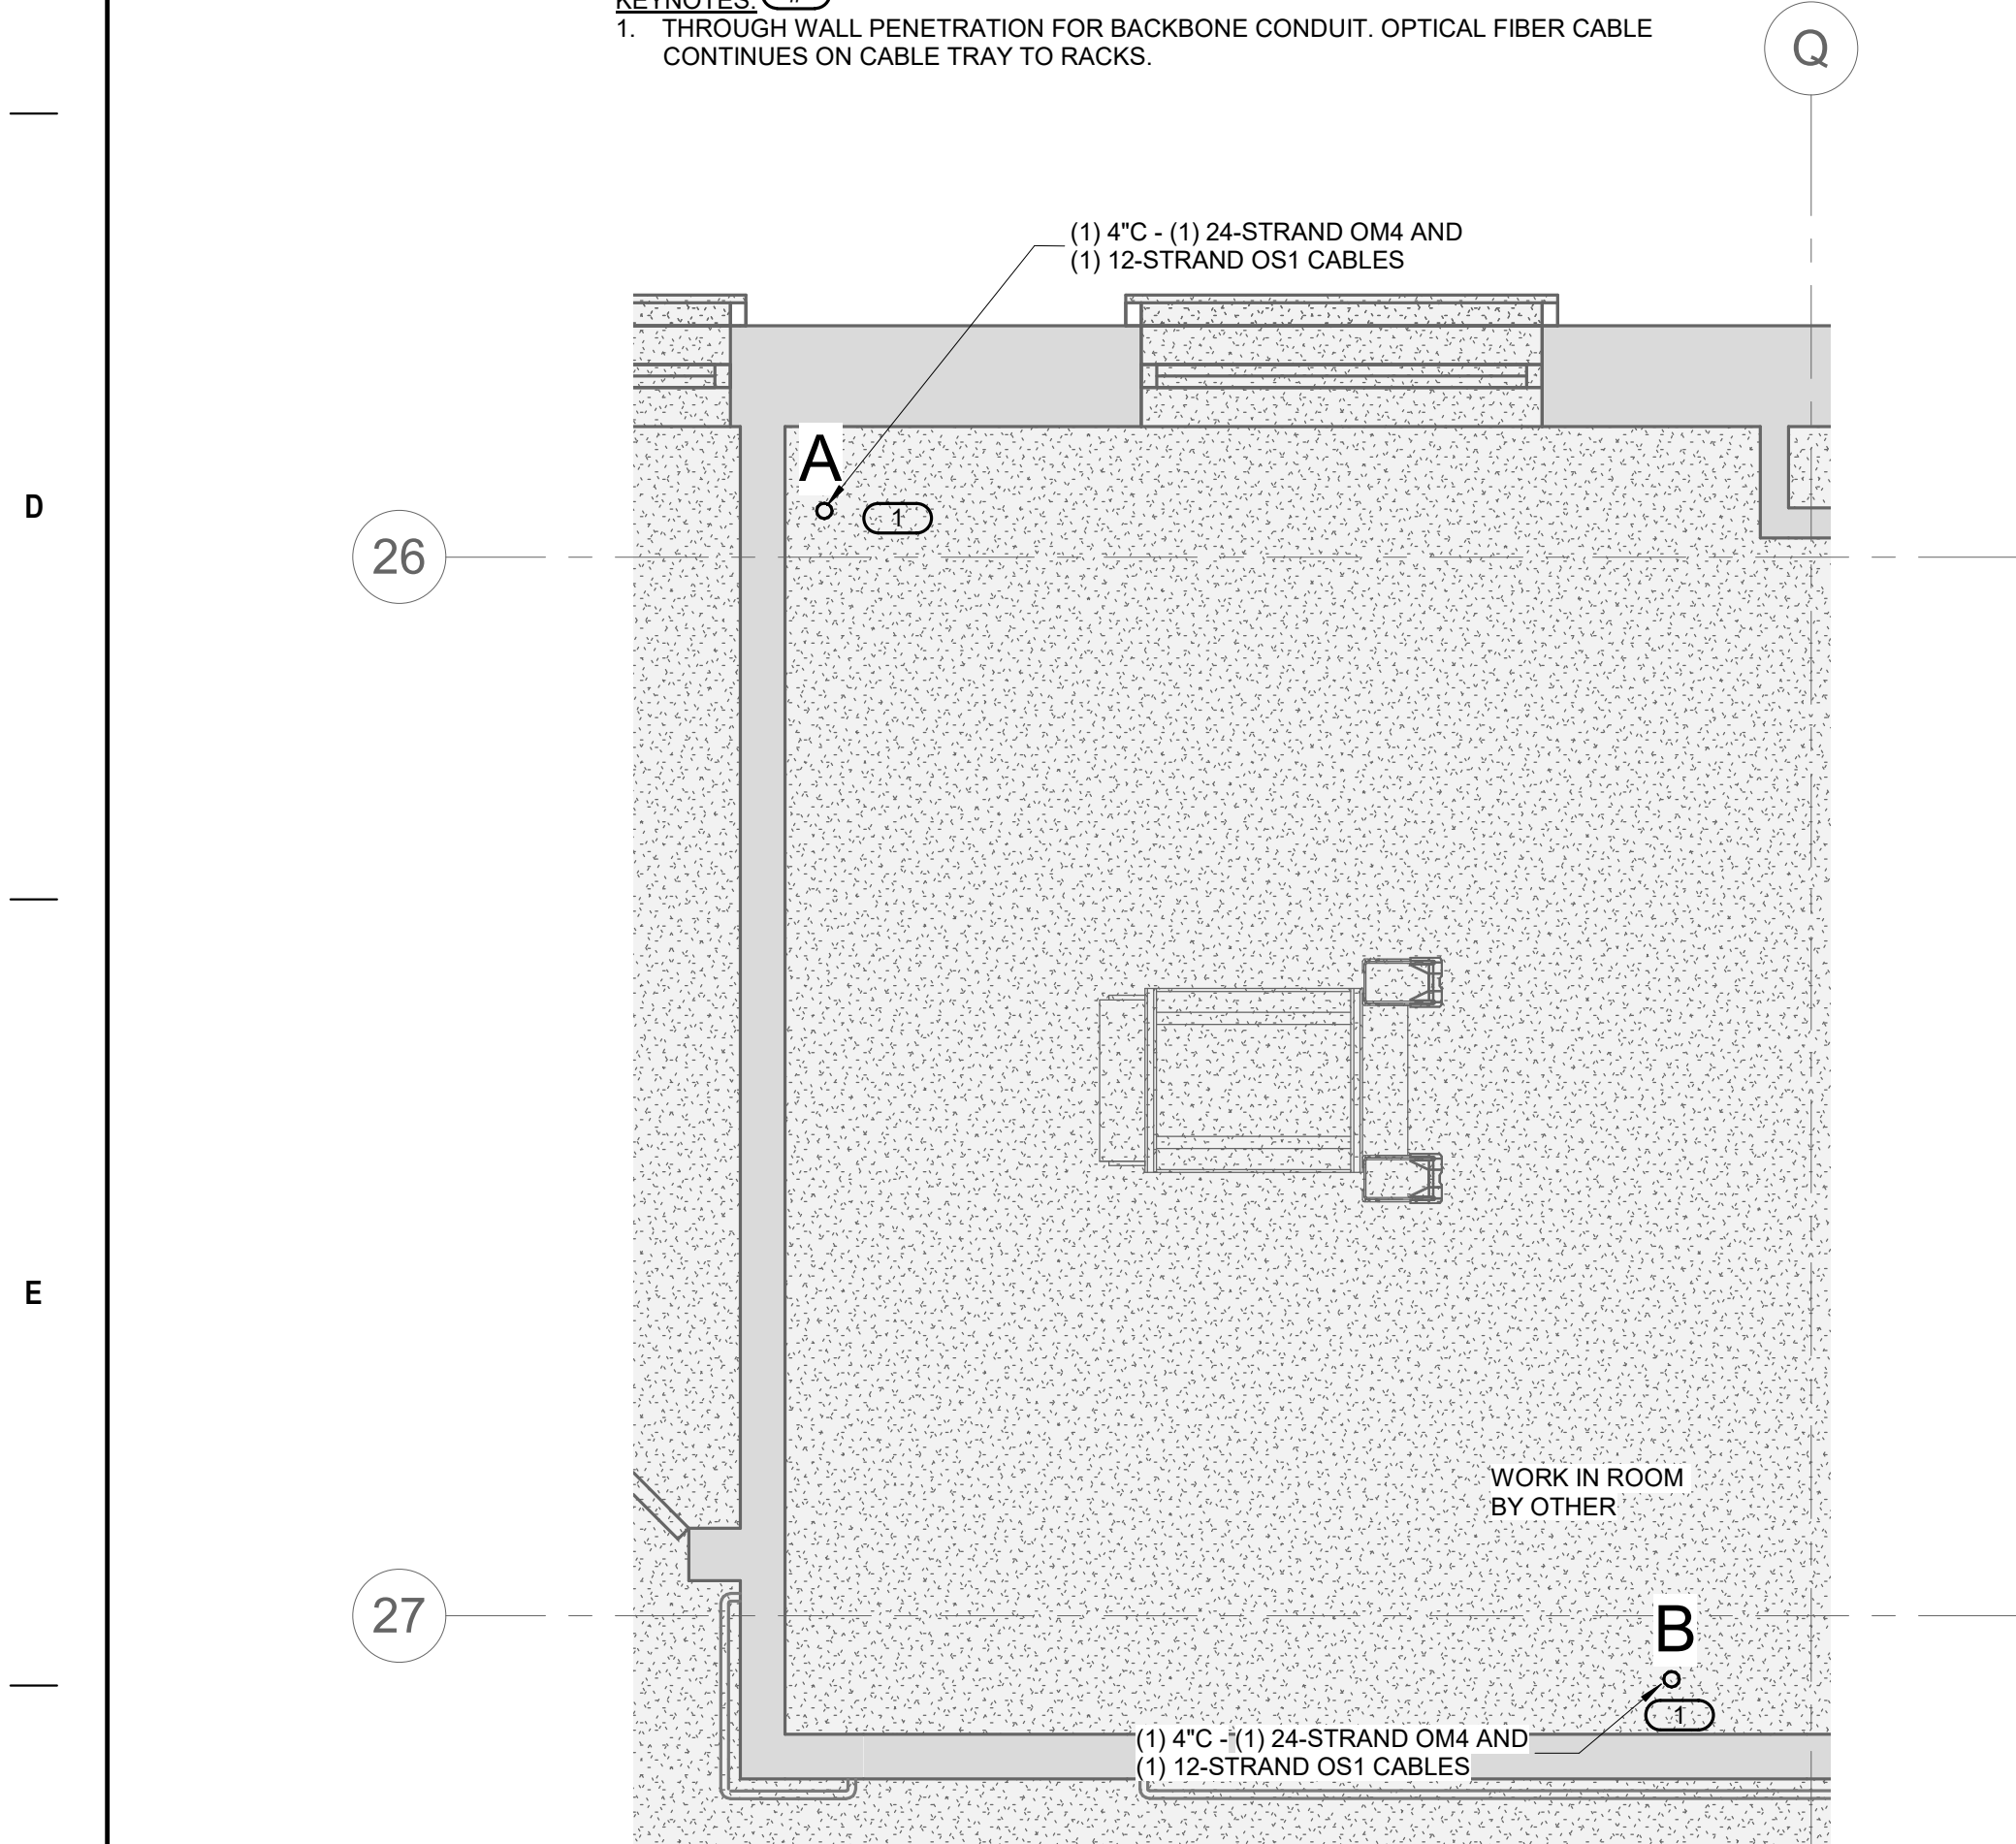

NORTH

3

1/2" = 1'-0"

TELECOM ROOM ENLARGEMENT TR #C506

NOTES:

1. REFER TO ELECTRICAL DRAWINGS FOR ROOM LAYOUT AND RACK ELEVATIONS.

2. ROUTE OPTICAL FIBER CABLE TO OVERHEAD CABLE TRAY AND TERMINATE IN FIBER DISTRIBUTION CABINET.

KEYNOTES: **#**

1. THROUGH WALL PENETRATION FOR BACKBONE CONDUIT. OPTICAL FIBER CABLE CONTINUES ON CABLE TRAY TO RACKS.

NORTH

4

1/2" = 1'-0"

TELECOM ROOM PATHWAY TR #C506

A


B

C

D

E

F

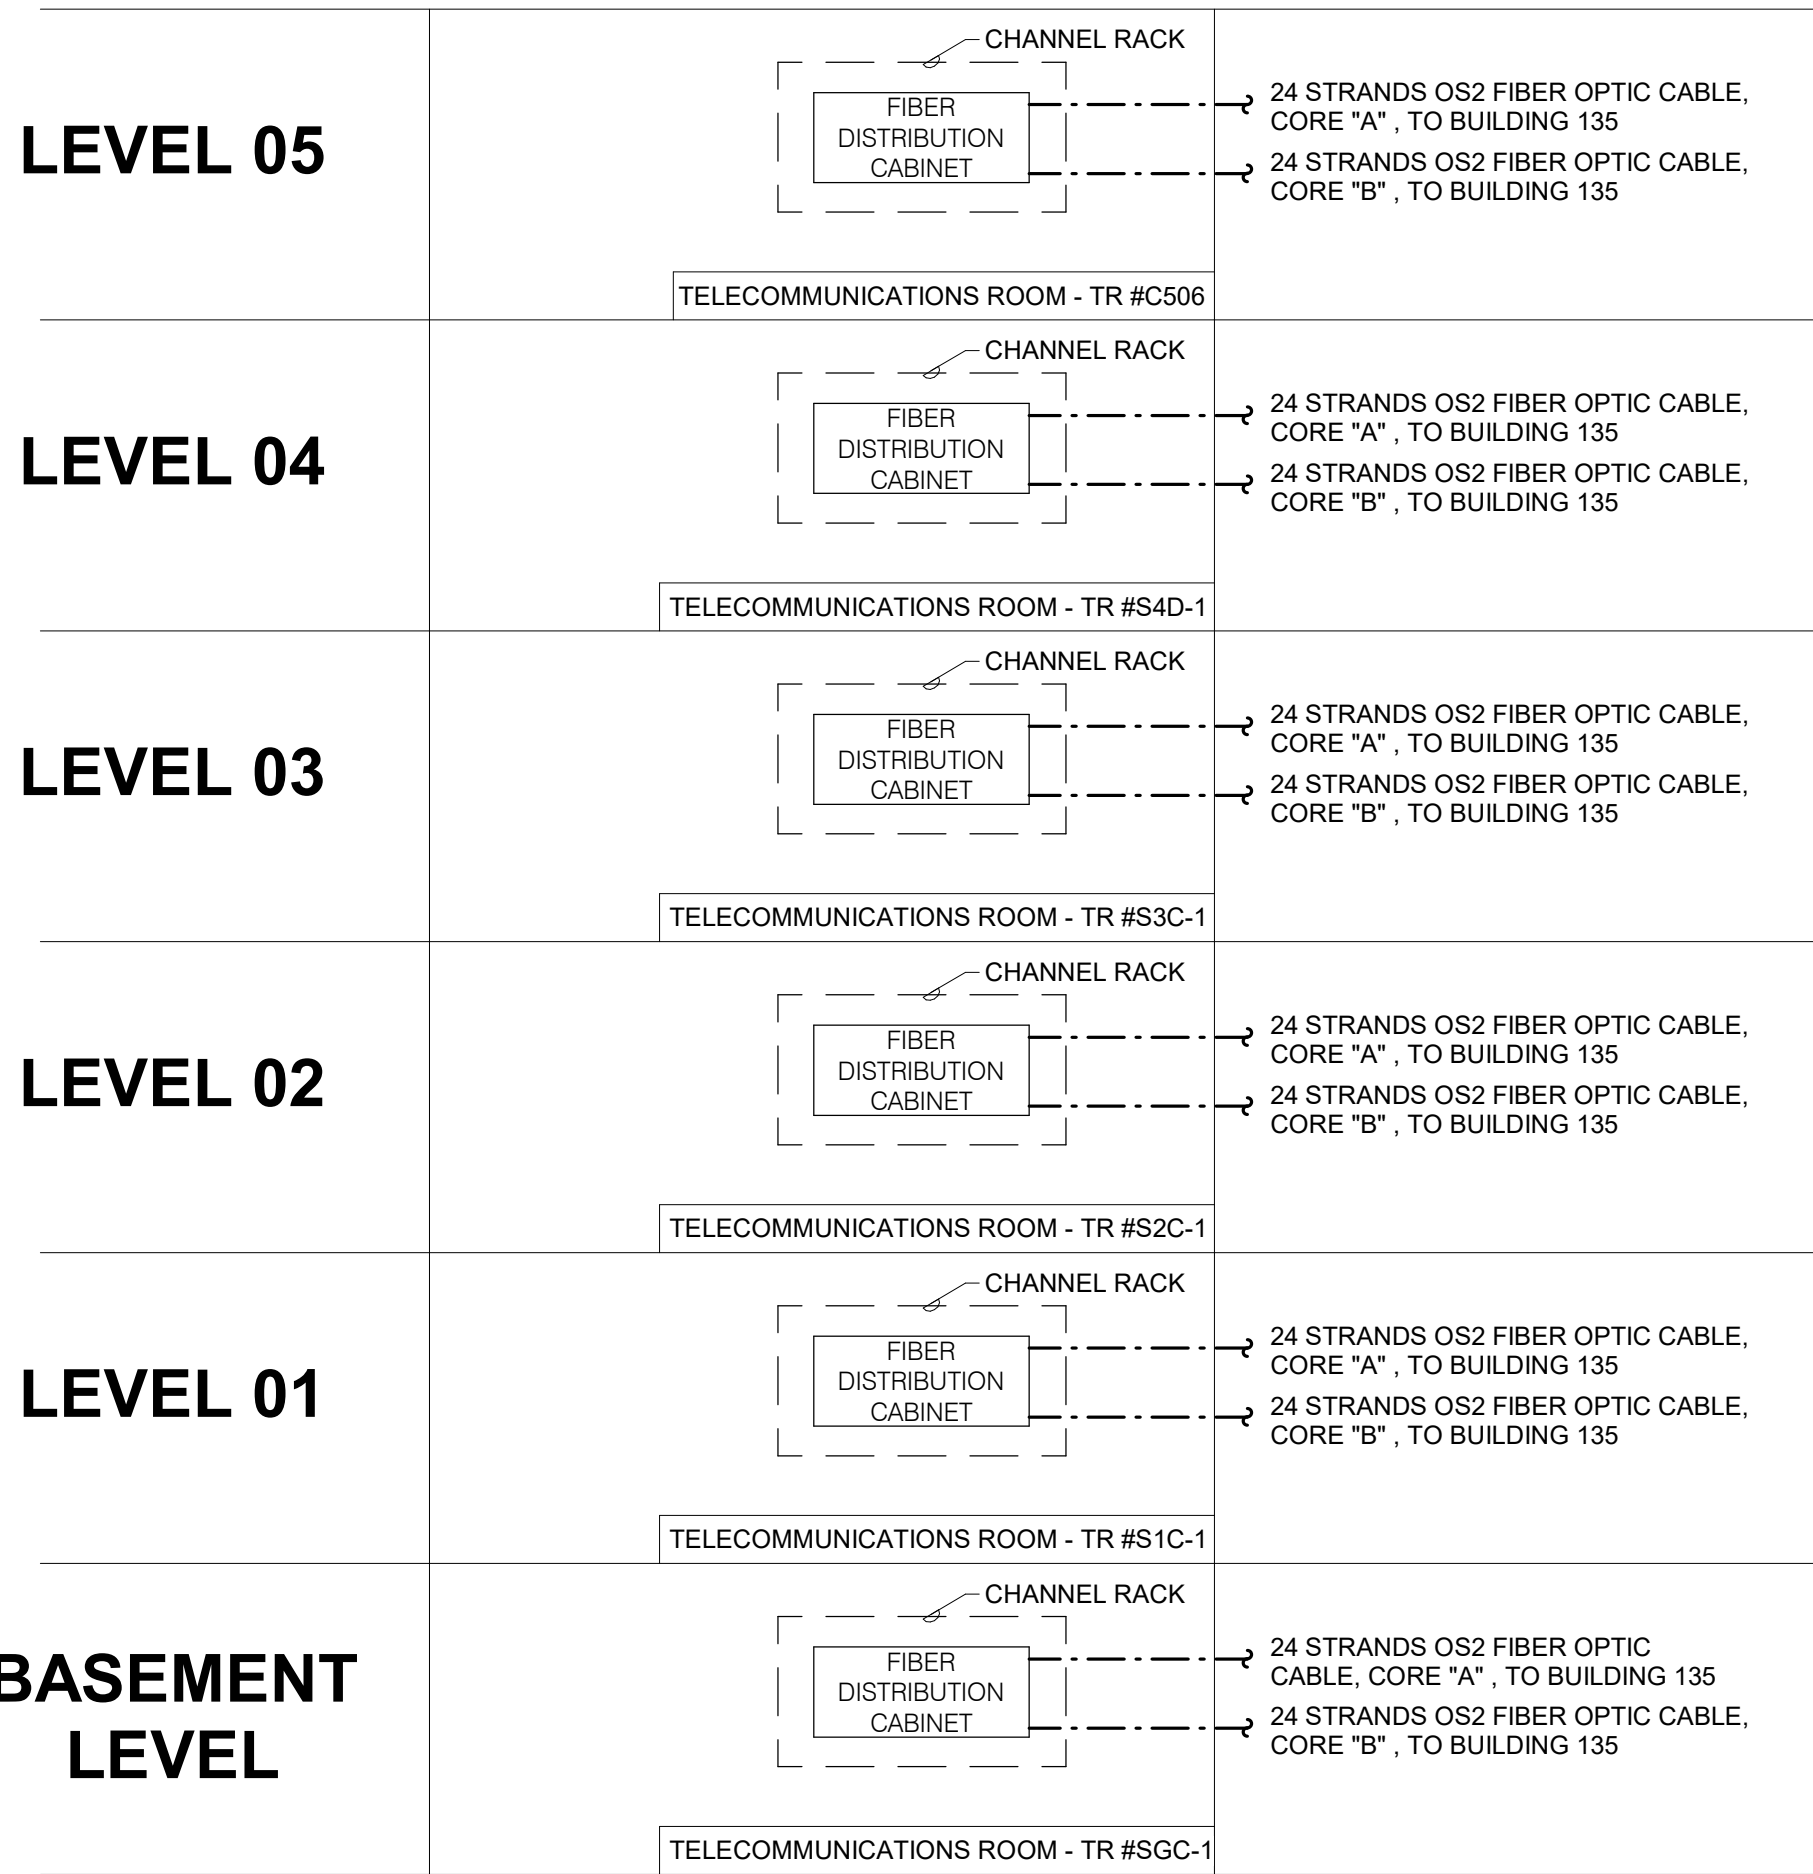

1

FIBER RISER DIAGRAM

- NO SCALE
- NOTES:
- THIS RISER IS DIAGRAMMATIC AND MAY NOT SHOW ACTUAL ROUTING OR QUANTITIES OF MATERIALS SHOWN. THIS RISER IS SHOWN FOR CLARIFICATION OF CONNECTION(S), LOCATIONS AND CABLE TYPE. ALL INFORMATION OUTLETS ARE TYPICAL OF THE OUTLETS IN THE AREA SHOWN. REFER TO FLOOR PLANS FOR MORE SPECIFIC ROUTING INFORMATION. REFER TO SPECIFICATIONS FOR ADDITIONAL REQUIREMENTS.
 - REFER TO ELECTRICAL DRAWINGS FOR CHANNEL RACK AND FIBER OPTIC DISTRIBUTION CABINET SPECIFICATIONS.

A


B

C

D

E

F

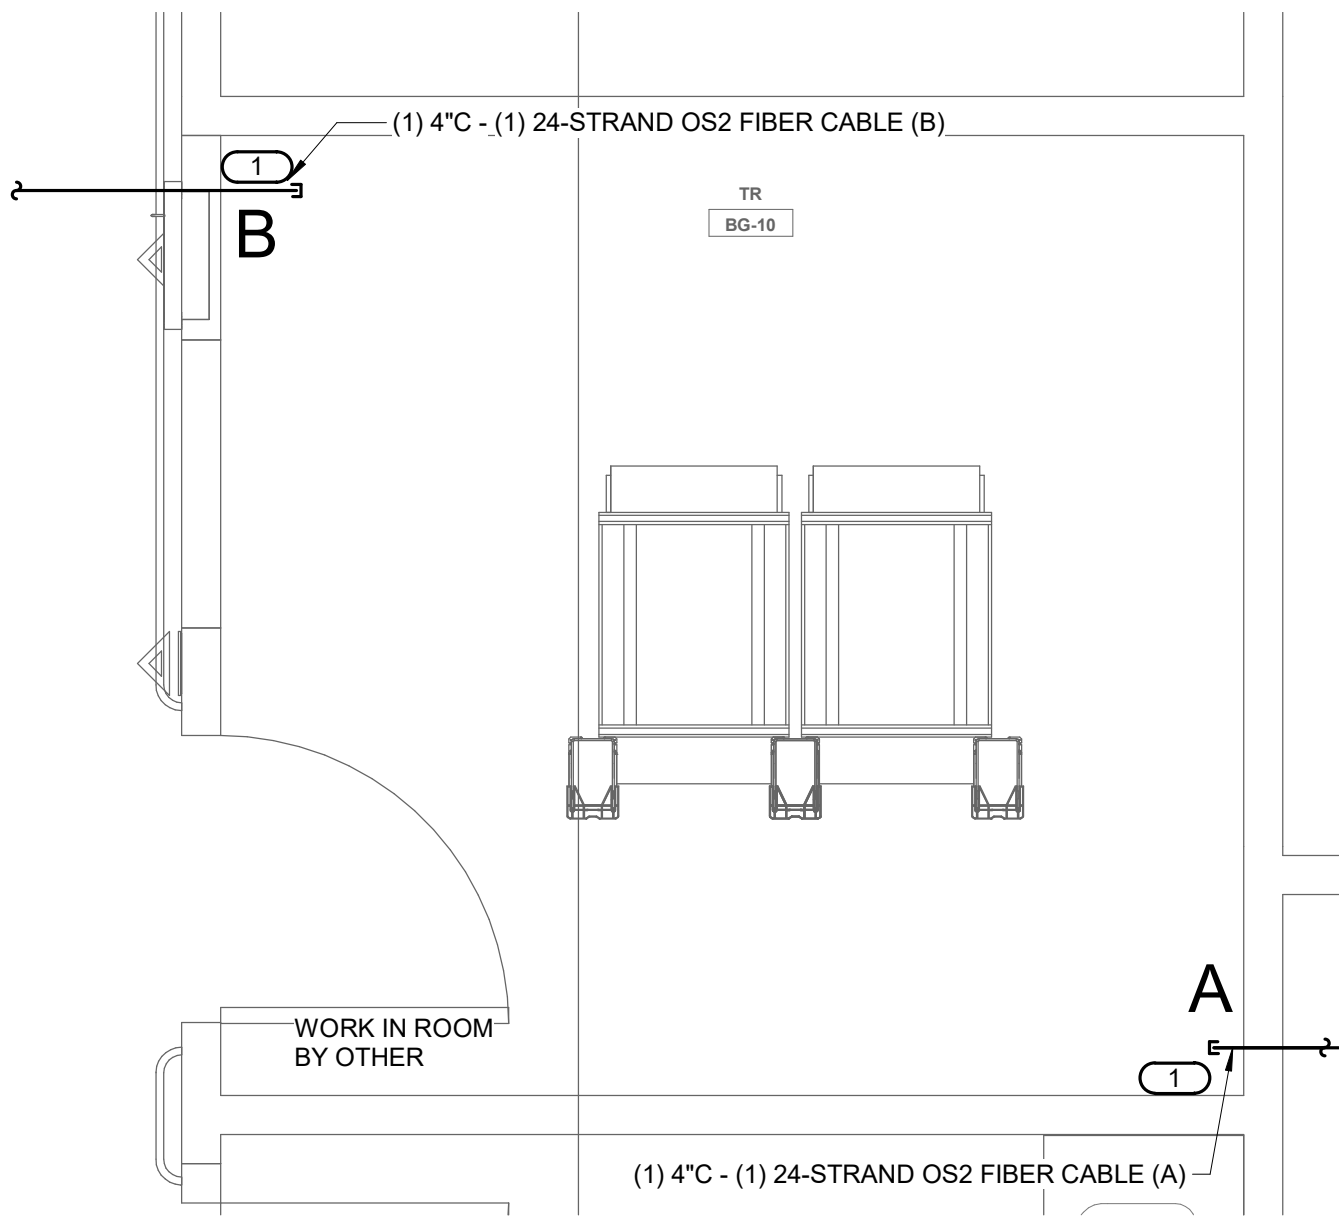


1 TELECOM ROOM ENLARGEMENT TR #BG10
1/2" = 1'-0"

NOTES:


- REFER TO ELECTRICAL DRAWINGS FOR ROOM LAYOUT AND RACK ELEVATIONS.
- ROUTE OPTICAL FIBER CABLE TO OVERHEAD CABLE TRAY AND TERMINATE IN FIBER DISTRIBUTION CABINET.

KEY NOTES: (B)

- THROUGH WALL PENETRATION FOR BACKBONE CONDUIT. OPTICAL FIBER CABLE CONTINUES ON CABLE TRAY TO RACKS.

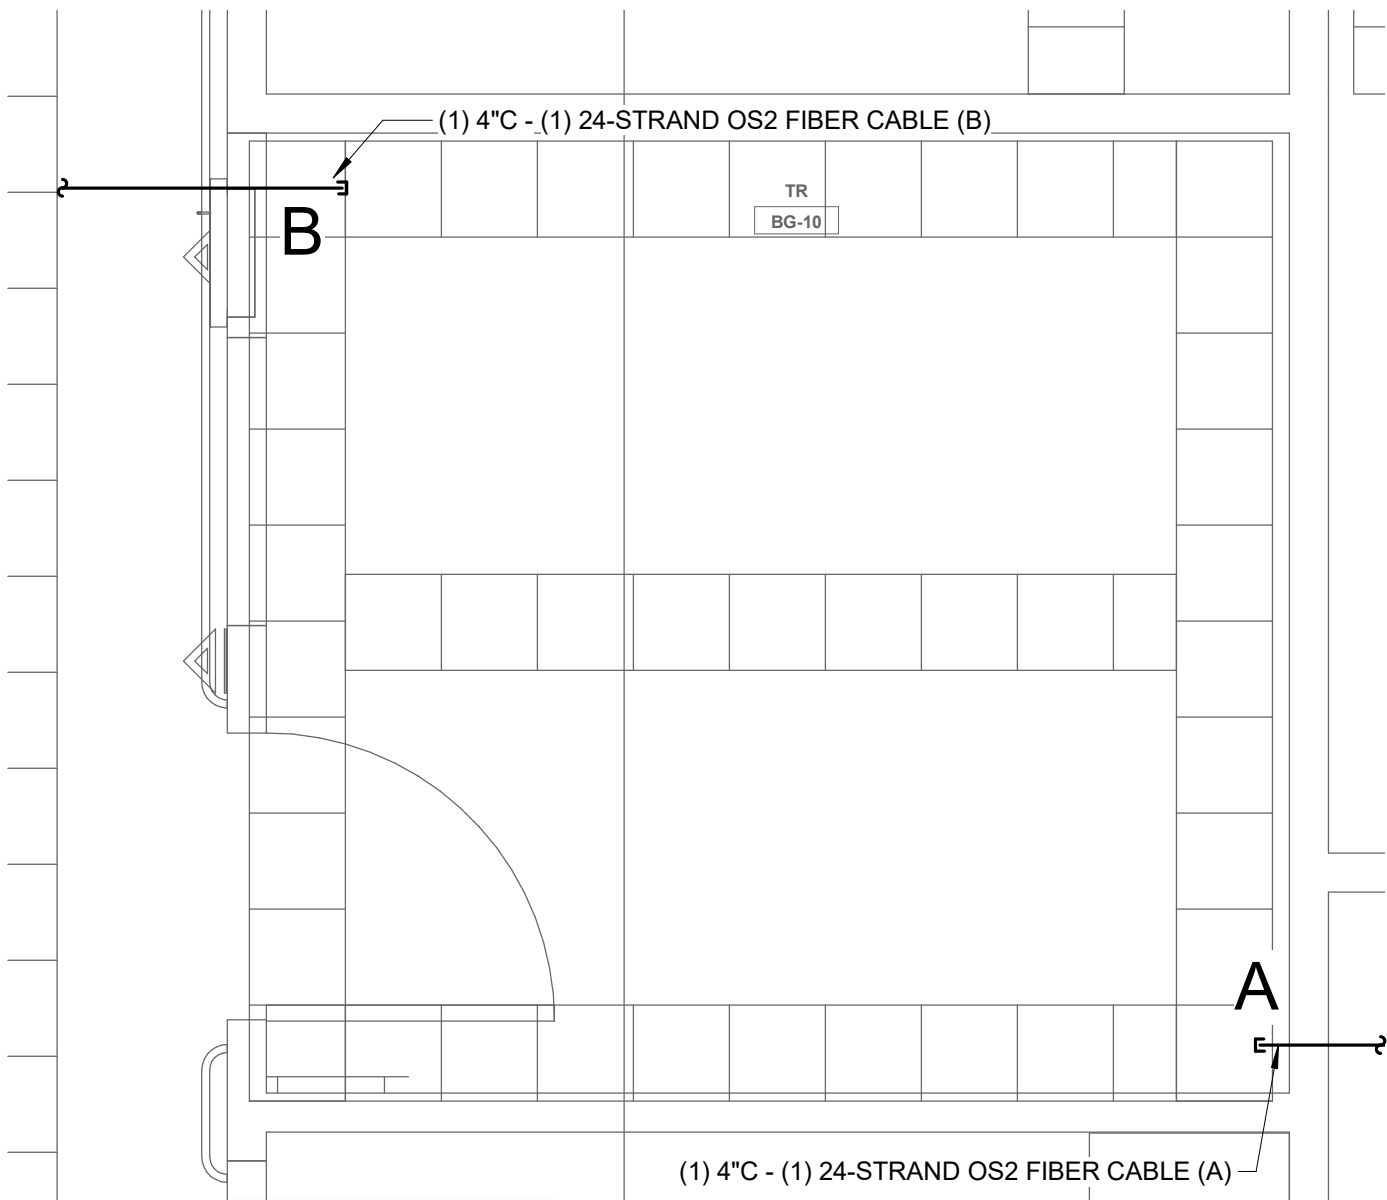

2 TELECOMROOM PATHWAY TR #BG10
1/2" = 1'-0"

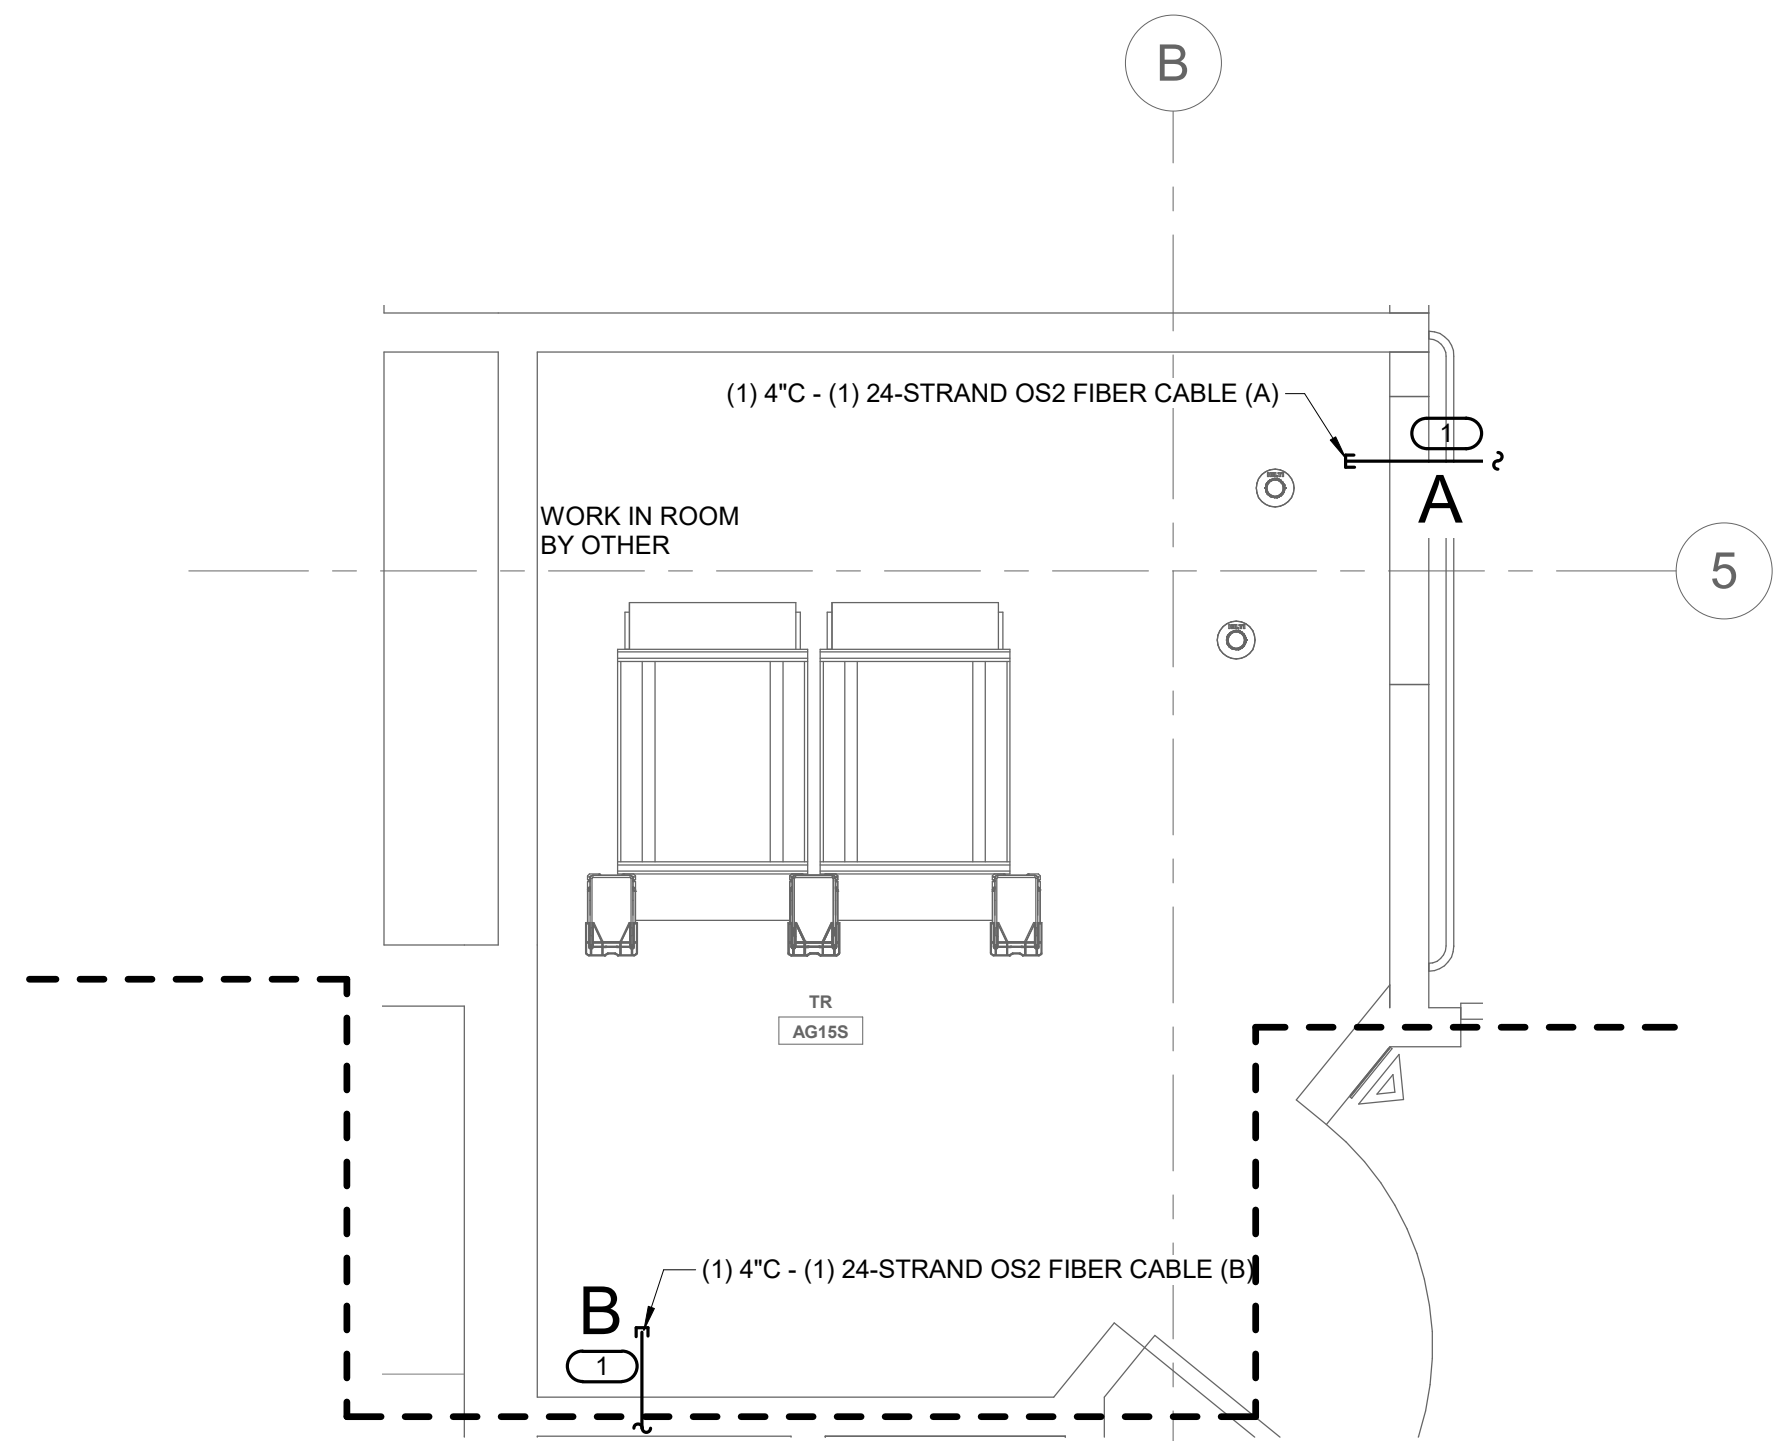


3 TELECOM ROOM ENLARGEMENT TR #AG15S
1/2" = 1'-0"

NOTES:


- REFER TO ELECTRICAL DRAWINGS FOR ROOM LAYOUT AND RACK ELEVATIONS.
- ROUTE OPTICAL FIBER CABLE TO OVERHEAD CABLE TRAY AND TERMINATE IN FIBER DISTRIBUTION CABINET.

KEY NOTES: (B)

- THROUGH WALL PENETRATION FOR BACKBONE CONDUIT. OPTICAL FIBER CABLE CONTINUES ON CABLE TRAY TO RACKS.

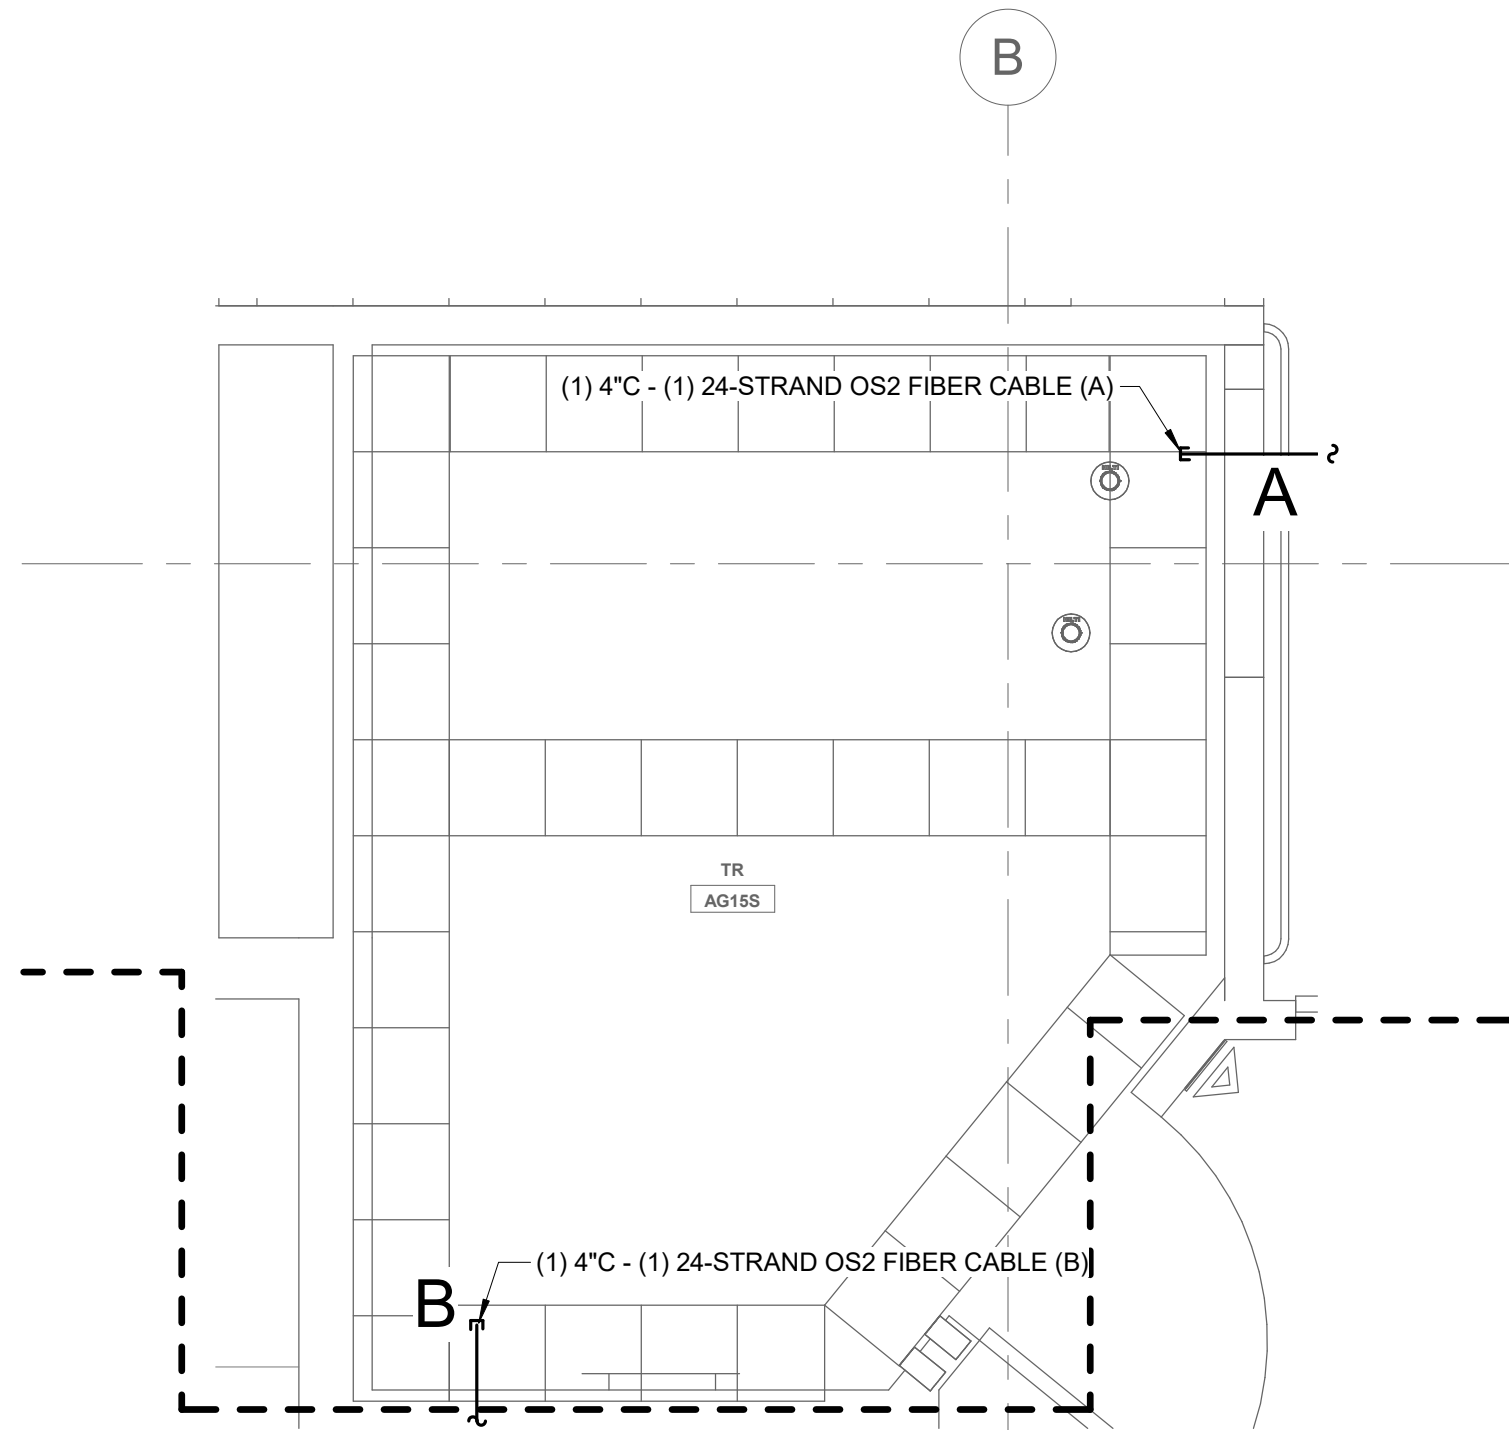


4 TELECOM ROOM PATHWAY TR #AG15S
1/2" = 1'-0"

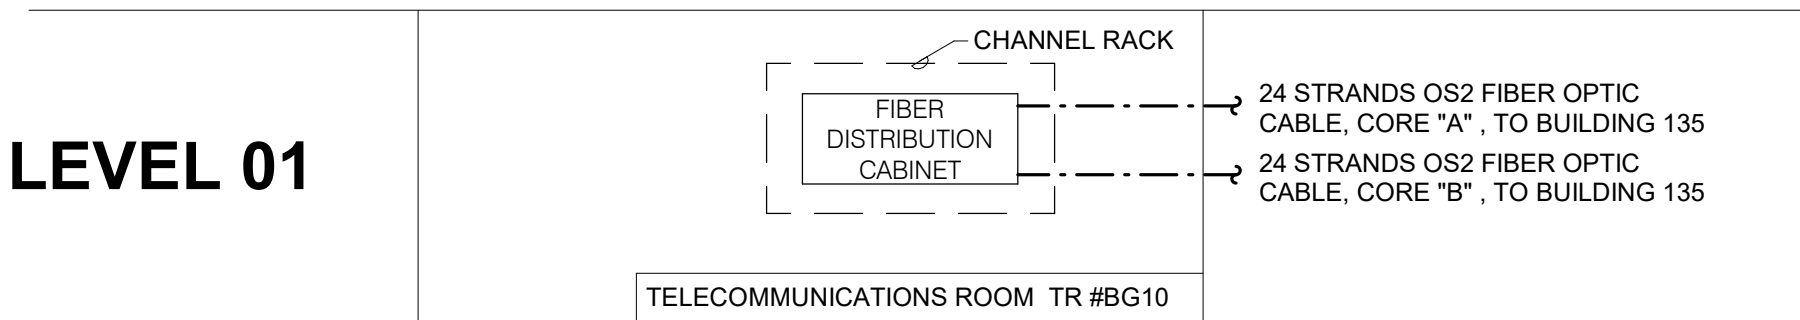

5 FIBER RISER DIAGRAM
NO SCALE

NOTES:

- THIS RISER IS DIAGRAMMATIC AND MAY NOT SHOW ACTUAL ROUTING OR QUANTITIES OF MATERIALS SHOWN. THIS RISER IS SHOWN FOR CLARIFICATION OF CONNECTION(S), LOCATIONS AND CABLE TYPE. ALL INFORMATION OUTLETS ARE TYPICAL OF THE OUTLETS IN THE AREA SHOWN. REFER TO FLOOR PLANS FOR MORE SPECIFIC ROUTING INFORMATION. REFER TO SPECIFICATIONS FOR ADDITIONAL REQUIREMENTS.
- REFER TO ELECTRICAL DRAWINGS FOR CHANNEL RACK AND FIBER OPTIC DISTRIBUTION CABINET SPECIFICATIONS

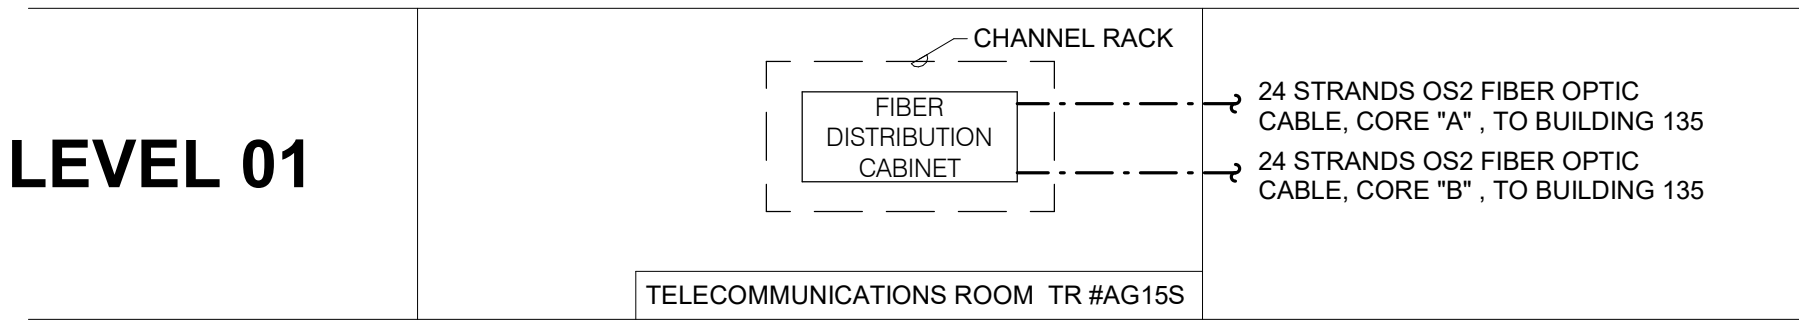

6 FIBER RISER DIAGRAM
NO SCALE


NOTES:

- THIS RISER IS DIAGRAMMATIC AND MAY NOT SHOW ACTUAL ROUTING OR QUANTITIES OF MATERIALS SHOWN. THIS RISER IS SHOWN FOR CLARIFICATION OF CONNECTION(S), LOCATIONS AND CABLE TYPE. ALL INFORMATION OUTLETS ARE TYPICAL OF THE OUTLETS IN THE AREA SHOWN. REFER TO FLOOR PLANS FOR MORE SPECIFIC ROUTING INFORMATION. REFER TO SPECIFICATIONS FOR ADDITIONAL REQUIREMENTS.
- REFER TO ELECTRICAL DRAWINGS FOR CHANNEL RACK AND FIBER OPTIC DISTRIBUTION CABINET SPECIFICATIONS

--	--	

- SHEET NOTES:**
- REFER TO SITE PLAN TS001 FOR ADDITIONAL INFORMATION.
 - REFER TO T500 AND T501 FOR CAMPUS OPTICAL FIBER CABLE RISER DIAGRAMS.
 - REFER TO 21400 FOR HANDHOLE DETAIL.
 - NEW BACKBONE OPTICAL FIBER CABLES SHALL BE INDOOR/OUTDOOR TYPE.
 - ALL BACKBONE OPTICAL FIBER CABLE PATHWAYS SHALL BE NEW. DO NOT RE-USE EXISTING BACKBONE CABLE PATHWAYS FOR NEW BACKBONE CABLES.
 - TRANSITION PVC CONDUITS TO GRC IN CRAWL SPACE OR EXPOSED EXTERIOR LOCATIONS. TRANSITION TO EMT CONDUITS AT INTERIOR OF BUILDING SEAL ALL PENETRATIONS TO MAINTAIN FIRE-RATINGS OF WALL, CEILING AND FLOORS.

- KEY NOTES:**
- PROVIDE PULLBOX ON EXTERIOR WALL AT HEIGHT OF CRAWL SPACE CEILING. ROUTE CONDUIT UP WALL INTO PULLBOX. PROVIDE PENETRATION AND ROUTE CONDUIT THRU PULLBOX INTO CRAWL SPACE. ROUTE CONDUIT IN CRAWL SPACE INTO CHASE AND UP TO ABOVE FIRST FLOOR CEILING. CONTINUE ROUTE ABOVE CEILING TO LOCATION BELOW EXISTING TR #A114.
 - PROVIDE PULLBOX ON EXTERIOR WALL AT HEIGHT OF CRAWL SPACE CEILING. ROUTE CONDUIT UP WALL INTO PULLBOX. PROVIDE PENETRATION AND ROUTE CONDUIT THRU PULLBOX INTO CRAWL SPACE. ROUTE CONDUIT IN CRAWL SPACE TO BELOW EXISTING TELECOM ROOM.
 - PROVIDE PENETRATION THRU FLOOR OF EXISTING TELECOM ROOM #AG03A AND ROUTE CONDUIT UP TO ABOVE CEILING. CONTINUE ROUTE ABOVE CEILING TO LOCATION BELOW EXISTING TR #A114.
 - PROVIDE PENETRATION THRU CEILING DECK AND ROUTE CONDUIT UP INTO TR #A114.

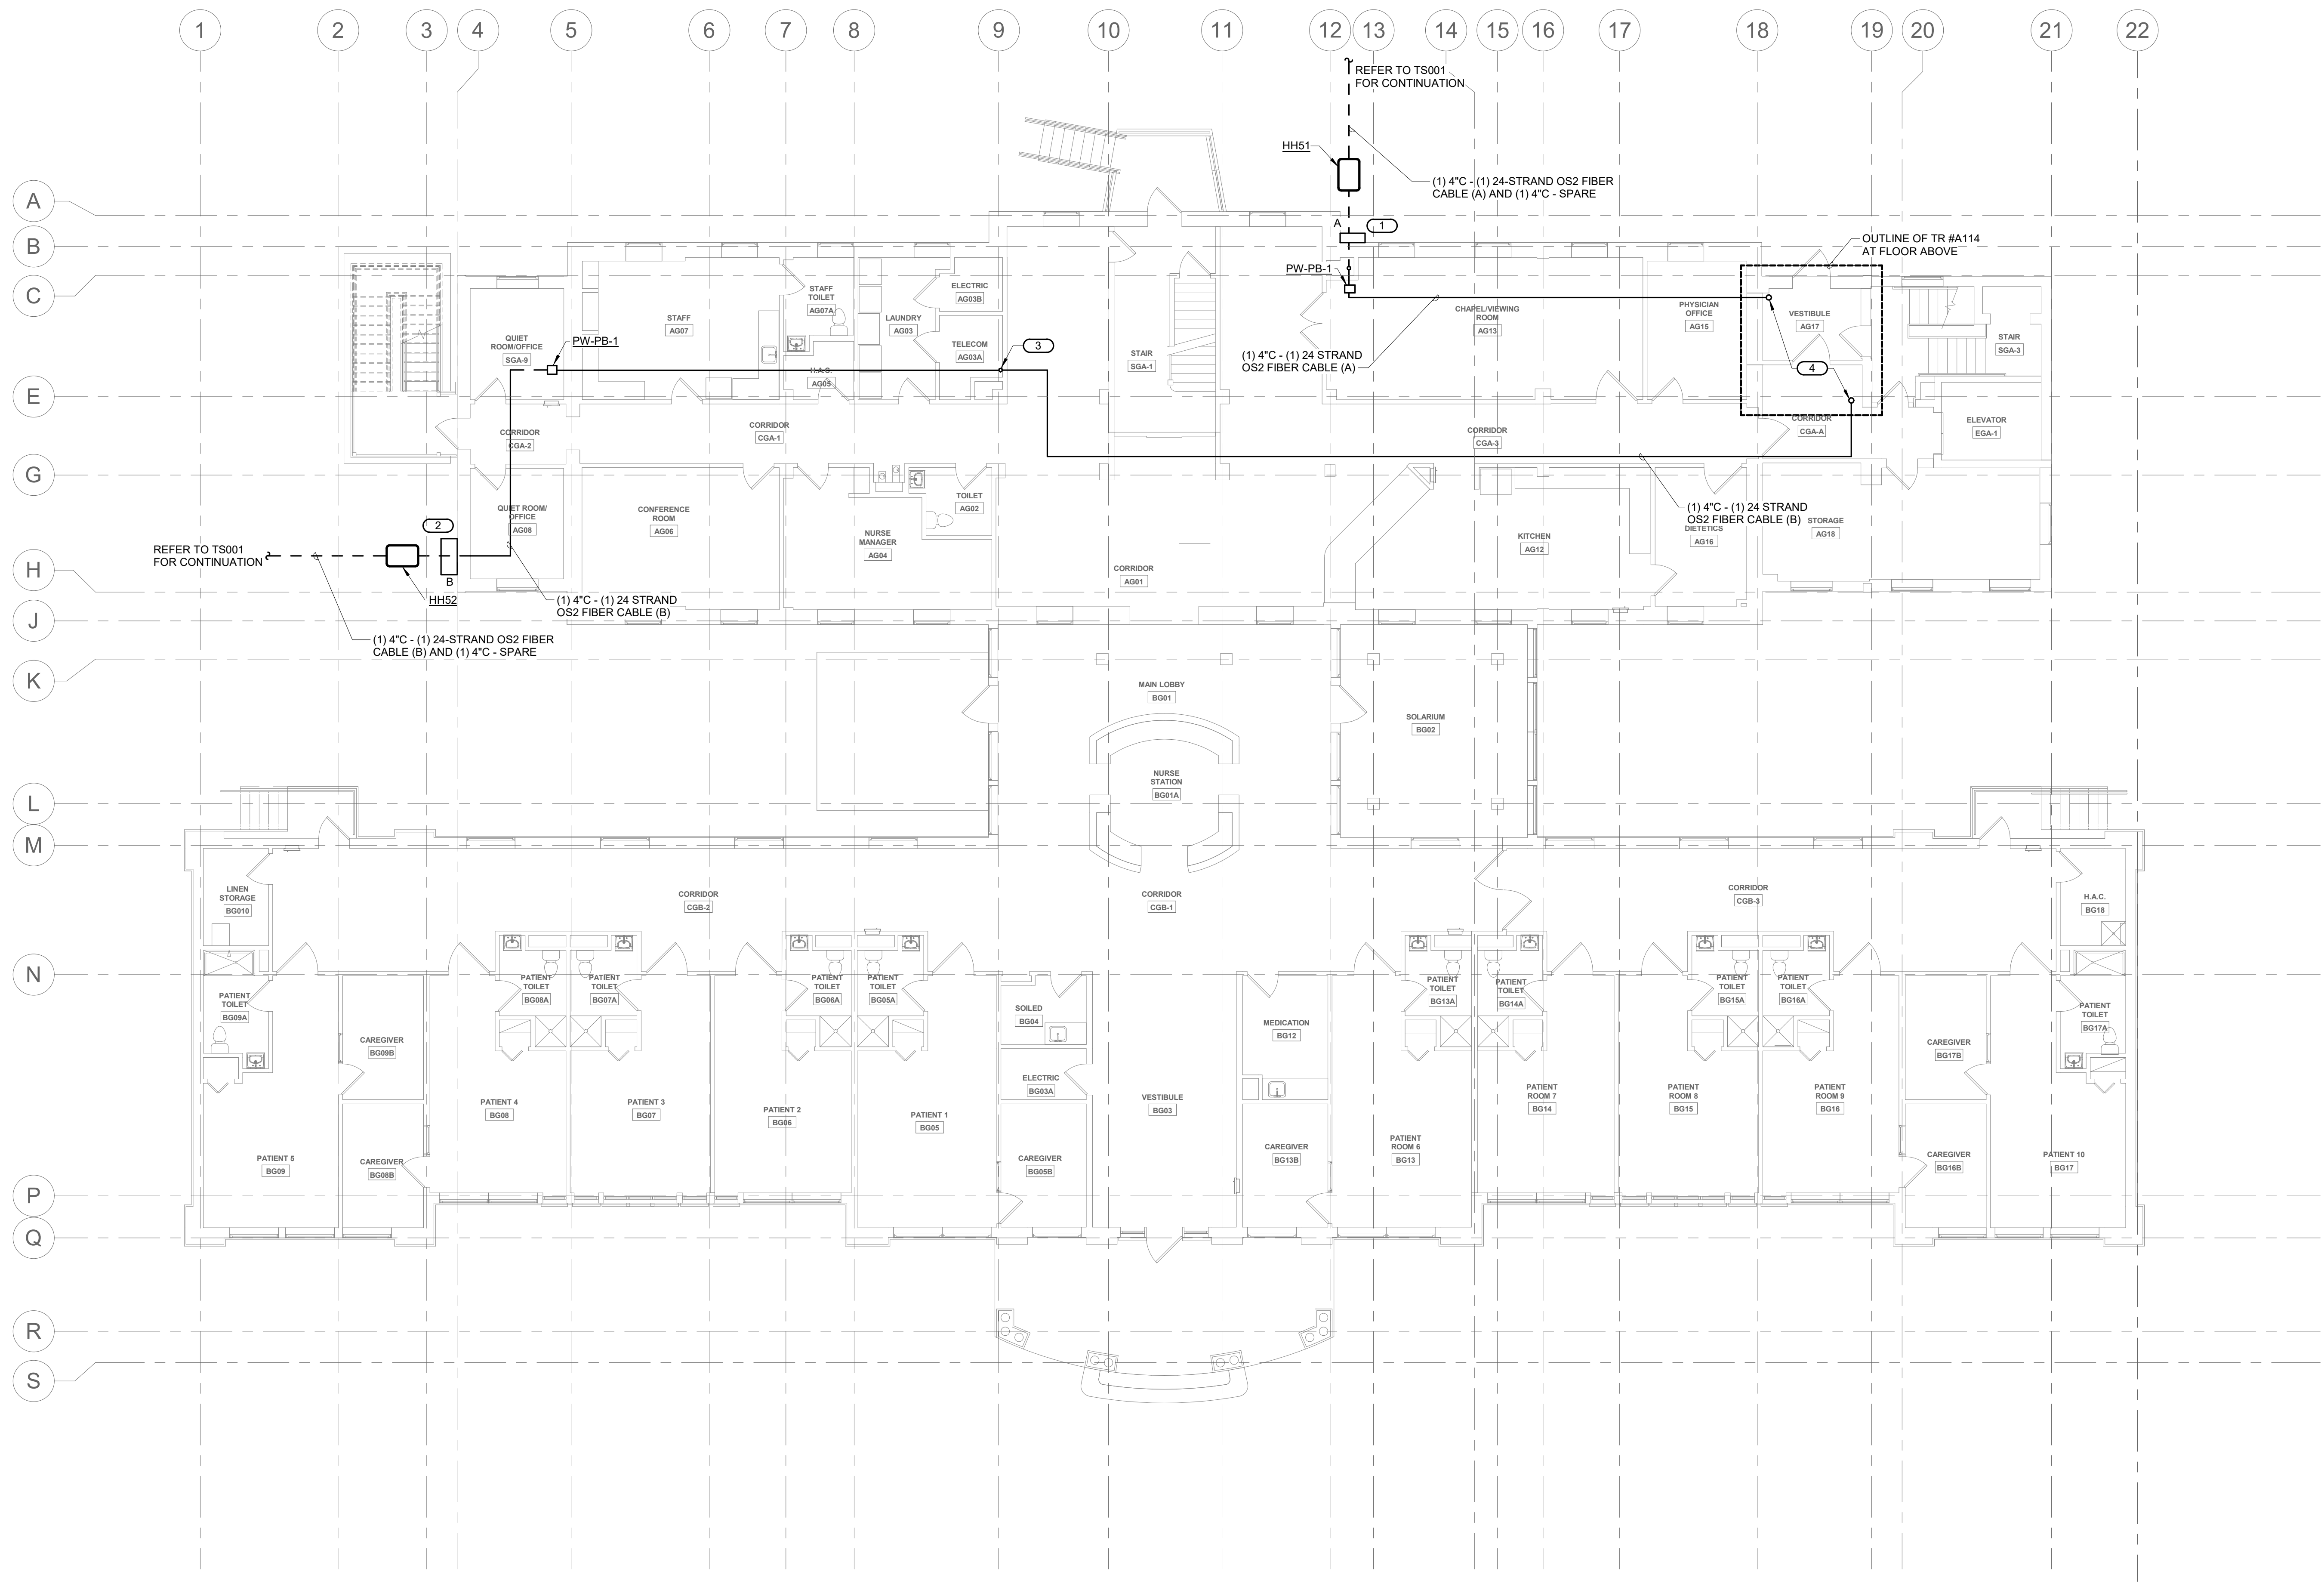


1 LEVEL 01 PLAN - TECHNOLOGY
1/8" = 1'-0"

8/13/2025 11:38:29 AM BLM 360/509-22-700 VHampton EHRM509-22-700.B114.T_021.rvt	</
--	--	----

- SHEET NOTES:**
1. REFER TO SITEPLAN TS001 FOR ADDITIONAL INFORMATION.
 2. REFER TO T500 AND T501 FOR CAMPUS OPTICAL FIBER CABLE RISER DIAGRAMS.
 3. REFER TO 2/T400 FOR HANDHOLE DETAIL.
 4. NEW BACKBONE OPTICAL FIBER CABLES SHALL BE INDOOR/OUTDOOR TYPE.
 5. ALL BACKBONE OPTICAL FIBER CABLE PATHWAYS SHALL BE NEW. DO NOT RE-USE EXISTING BACKBONE CABLE PATHWAYS FOR NEW BACKBONE CABLES.
 6. TRANSITION PVC CONDUITS TO GRC IN CRAWL SPACE OR EXPOSED EXTERIOR LOCATIONS. TRANSITION TO EMT CONDUITS AT INTERIOR OF BUILDING. SEAL ALL PENETRATIONS TO MAINTAIN FIRE-RATINGS OF WALL, CEILING AND FLOORS.

- KEYNOTES:** (#)
1. ROUTE CONDUIT UP THRU FLOOR OF TR #A114 AND CONTINUE TO HEIGHT ABOVE CABLE TRAY.

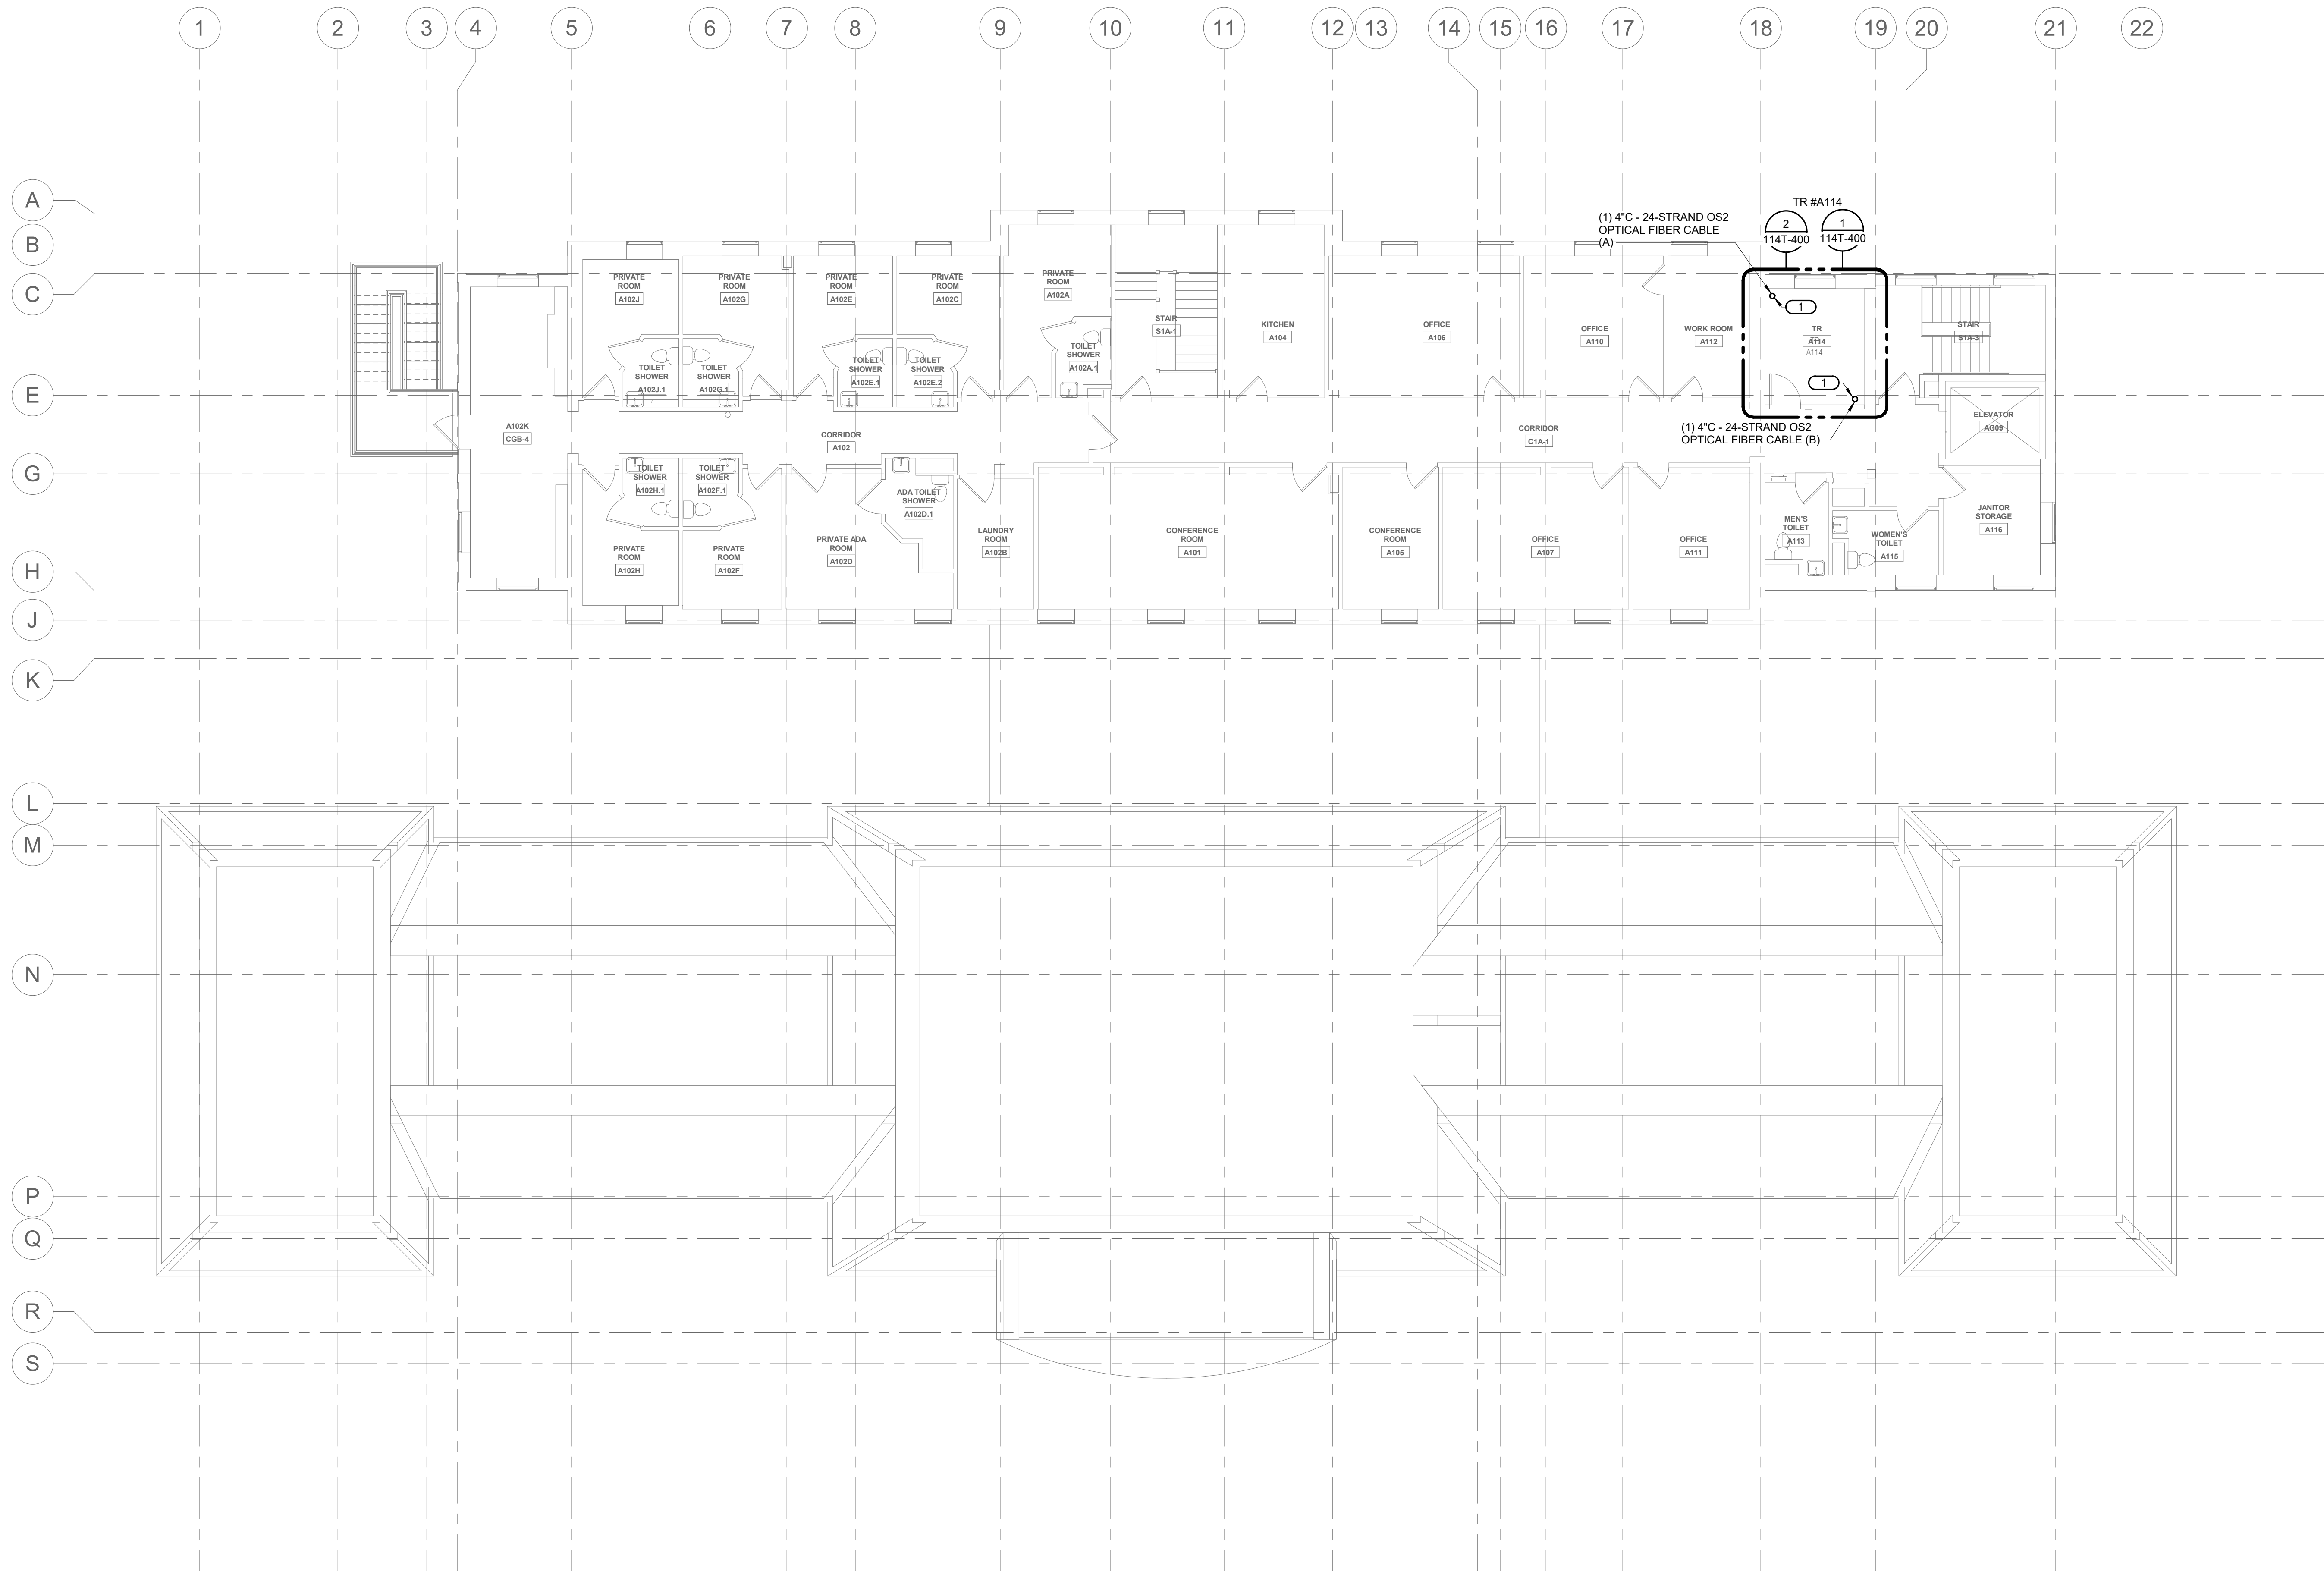

BLM 360/509-22-700
VAHampton
EHRM509-700.B114T_R2.rvt

8/13/2025 11:38:31 AM

VA FORM 08 - 6231

Revisions:	Date:

CONSULTANT
ENGINEERING DISCIPLINE:

225 W WASHINGTON STREET SUITE 2700 CHICAGO, IL 60609 P: 312.294.0501 F: 312.294.0003 PROJECT #22010109.00

ARCHITECT/ENGINEER OF RECORD
A/E:
SPEES DESIGN BUILD 23830 PACIFIC HIGHWAY S. SUITE 203 KENT, WA 98032
 SPEESDESIGNBUILD

STAMP


Office of Construction and Facilities Management
 U.S. Department of Veterans Affairs

Drawing Title
BLDG.114 TECHNOLOGY ENLARGED PLANS
Approved:

Phase
100% CONSTRUCTION DOCUMENTS
FULLY SPRINKLERED


Project Title
EHRM INFRASTRUCTURE UPGRADES - HAMPTON
Location
HAMPTON VA MEDICAL CENTER, HAMPTON, VIRGINIA
Issue Date
05/09/2025
Checked
EW
Drawn
IMEG

Project Number
509-22-700
Building Number
114
Drawing Number
114T-400
688 of 713

[illegible]


A
B
C
D
E
F

A
B
C
D
E
F

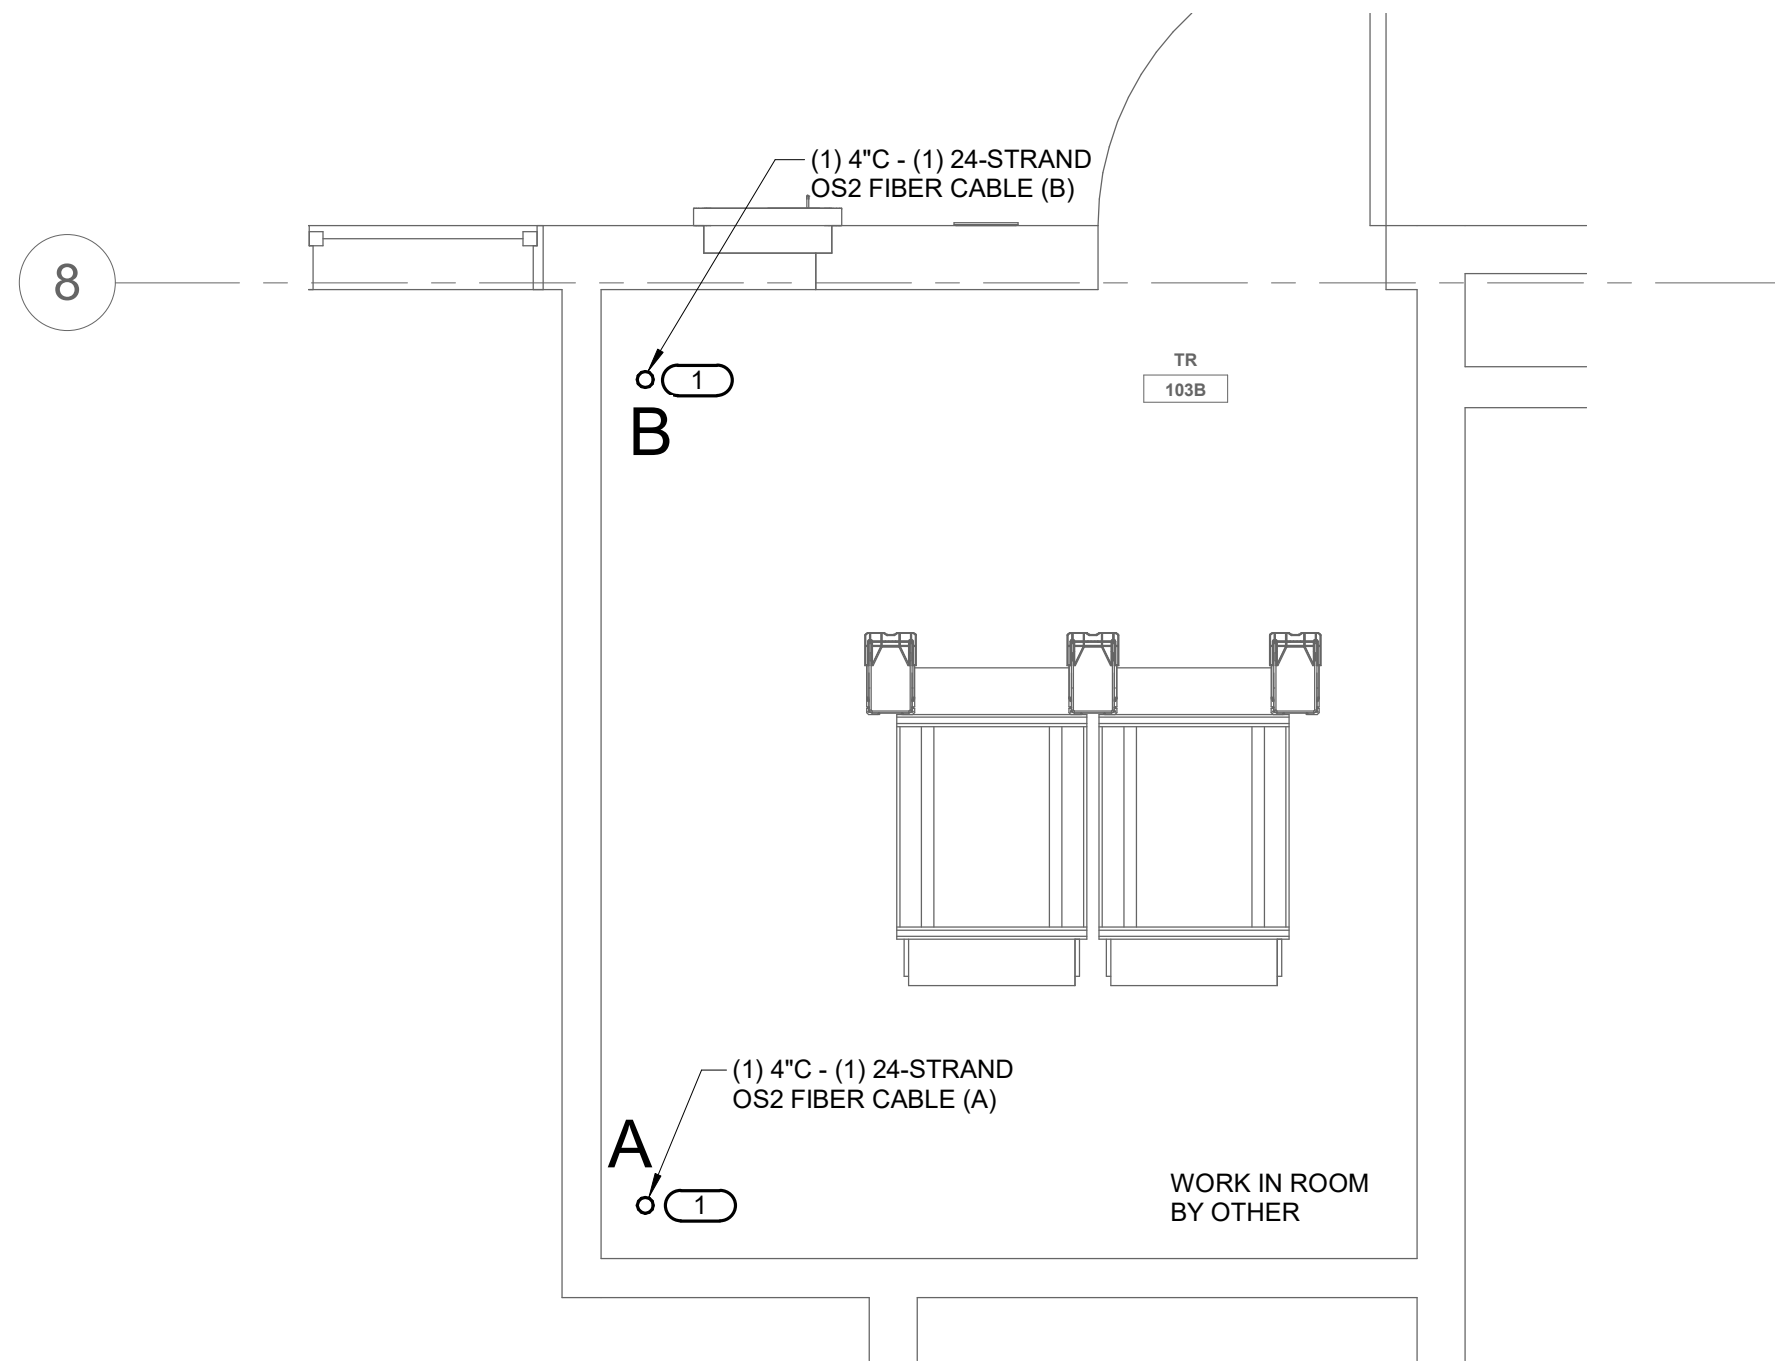


1 TELECOM ROOM ENLARGEMENT TR #103B
1/2" = 1'-0"
NOTES:
1. REFER TO ELECTRICAL DRAWINGS FOR ROOM LAYOUT AND RACK ELEVATIONS.
2. ROUTE OPTICAL FIBER CABLE TO OVERHEAD CABLE TRAY AND TERMINATE IN FIBER DISTRIBUTION CABINET.
KEY NOTES: (B)
1. THROUGH FLOOR PENETRATION FOR BACKBONE CONDUIT. OPTICAL FIBER CABLE CONTINUES ON CABLE TRAY TO RACKS.

POT PAN
WASH
103C

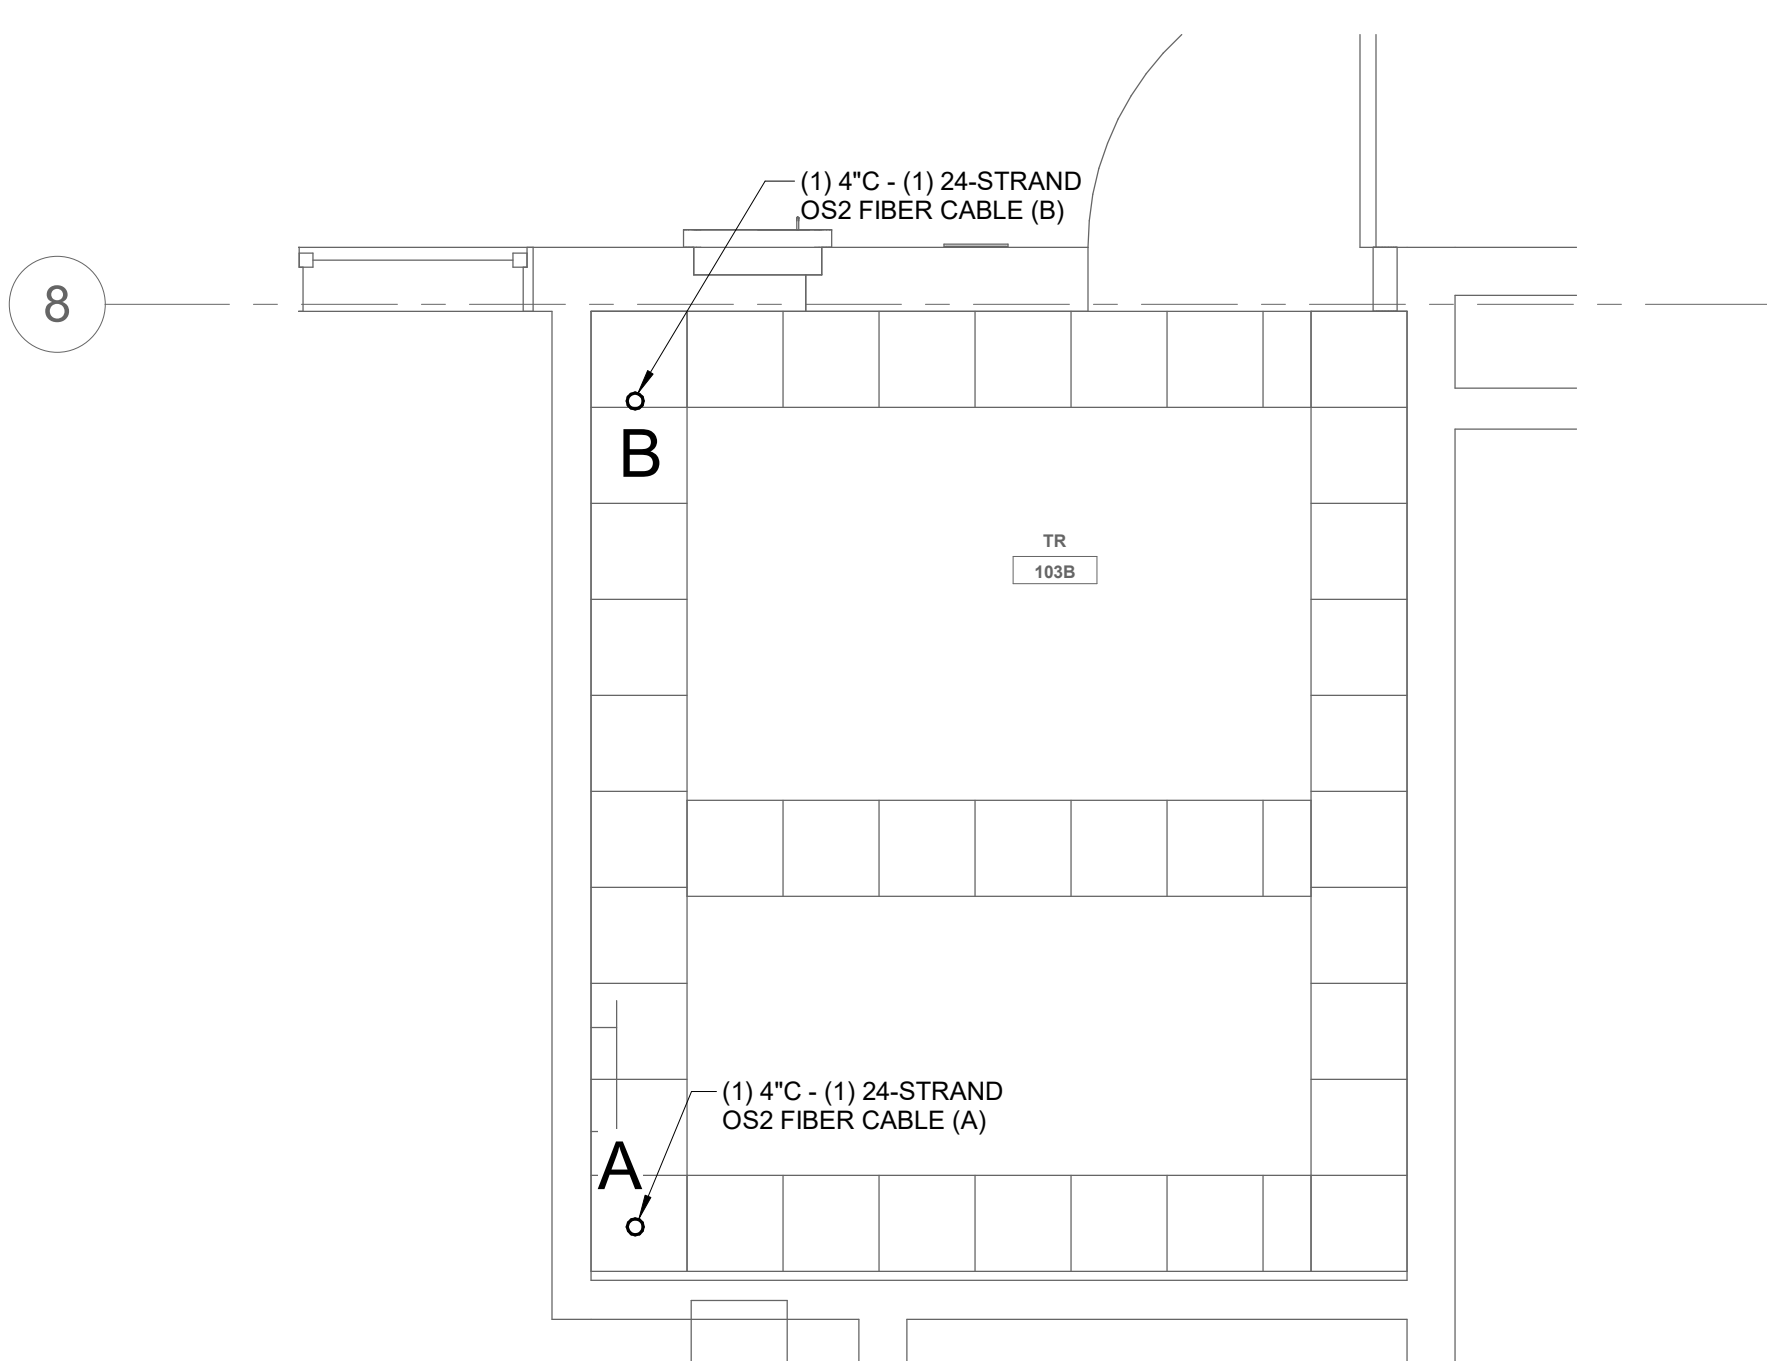

2 TELECOM ROOM PATHWAY TR #103B
1/2" = 1'-0"

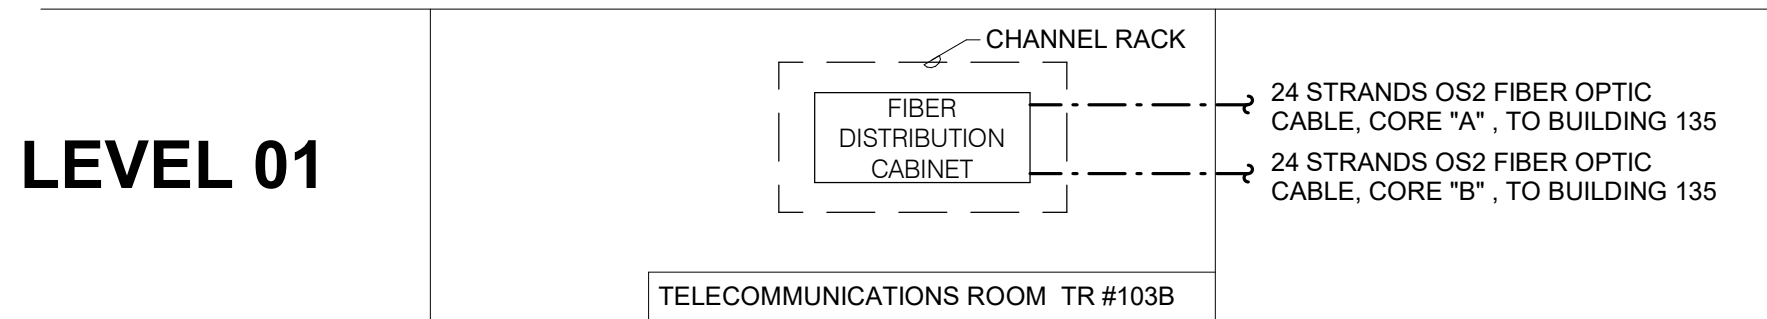

3 FIBER RISER DIAGRAM
NO SCALE
NOTES:
1. THIS RISER IS DIAGRAMMATIC AND MAY NOT SHOW ACTUAL ROUTING OR QUANTITIES OF MATERIALS SHOWN. THIS RISER IS SHOWN FOR CLARIFICATION OF CONNECTION(S), LOCATIONS AND CABLE TYPE. ALL INFORMATION OUTLETS ARE TYPICAL OF THE OUTLETS IN THE AREA SHOWN. REFER TO FLOOR PLANS FOR MORE SPECIFIC ROUTING INFORMATION. REFER TO SPECIFICATIONS FOR ADDITIONAL REQUIREMENTS.
2. REFER TO ELECTRICAL DRAWINGS FOR CHANNEL RACK AND FIBER OPTIC DISTRIBUTION CABINET SPECIFICATIONS


Revisions:	Date:	CONSULTANT ENGINEERING DISCIPLINE: IMEG www.imegcorp.com 225 W WASHINGTON STREET SUITE 2700 CHICAGO, IL 60606 P: 312.294.0501 F: 312.294.0003 PROJECT #22010109.00	ARCHITECT/ENGINEER OF RECORD A/E: SDB SPEESDESIGNBUILD 23830 PACIFIC HIGHWAY S. SUITE 203 KENT, WA 98032	STAMP Bicsi ES&C - VME - J Reg. No. 1919026 Expires 03/01/2025 RCDD	Office of Construction and Facilities Management VA U.S. Department of Veterans Affairs	Drawing Title BLDG.116 TECHNOLOGY ENLARGED PLANS	Phase 100% CONSTRUCTION DOCUMENTS	Project Title EHRM INFRASTRUCTURE UPGRADES - HAMPTON	Project Number 509-22-700
		Approved:	FULLY SPRINKLERED	Location HAMPTON VA MEDICAL CENTER, HAMPTON, VIRGINIA	Building Number 116				
		Issue Date 05/09/2025	Checked EW	Drawn IMEG	Drawing Number 116T-400				
					690 of 713				

SHEET NOTES

1. REFER TO SITEPLAN TS001 FOR ADDITIONAL INFORMATION.
2. REFER TO T500 AND 00-T501 FOR CAMPUS OPTICAL FIBER RISER DIAGRAMS.
3. REFER TO 2/T400 FOR HANDHOLE DETAIL.
4. REFER TO ENLARGED PLANS FOR ADDITIONAL INFORMATION.
5. ROUTES SHOWN THRU CRAWL SPACES ARE "SUGGESTED" ROUTES. FIELDVERIFY EXACT ROUTES.
6. SEAL ALL PENETRATIONS TO MAINTAIN FIRE-RATINGS OF WALL, CEILING AND FLOORS.


KEY NOTES: #

1. PROVIDE FIBERBOX AND PENETRATION THRU EXTERIOR WALL AND ROUTE CONDUITS INTO CRAWL SPACE AND CONTINUE TO LOCATION BELOW STORAGE RM. #AG22B.
2. PROVIDE PENETRATIONS THRU FLOOR OF STORAGE RM. #AG22B ABOUT 18" ABOVE EXISTING FLOOR GRADE ADJACENT TO EXISTING CONDUITS. STACK CONDUITS TO SAVE SPACE.
3. CONTINUE ROUTE OF CONDUITS TO ABOVE FINISHED FLOOR THROUGH CORRIDORS TO BLDG. 1B1.
4. PROVIDE PENETRATIONS THRU WALL OF BLDG. #135 AND ROUTE CONDUITS ABOVE FIRST FLOOR CEILING OF WORK RM. #168. REFER TO BLDG #168 PLANS FOR ADDITIONAL WORK REQUIREMENTS.
5. PROVIDE (2) 24 STRAND OM3 OPTICAL FIBER CABLES BETWEEN EXISTING CORE SWITCHES AND NEW CORE SWITCHES IN EXISTING MAIN COMPUTER ROOM #AG10. SEE ENLARGED PLAN FOR ADDITIONAL WORK REQUIREMENTS.

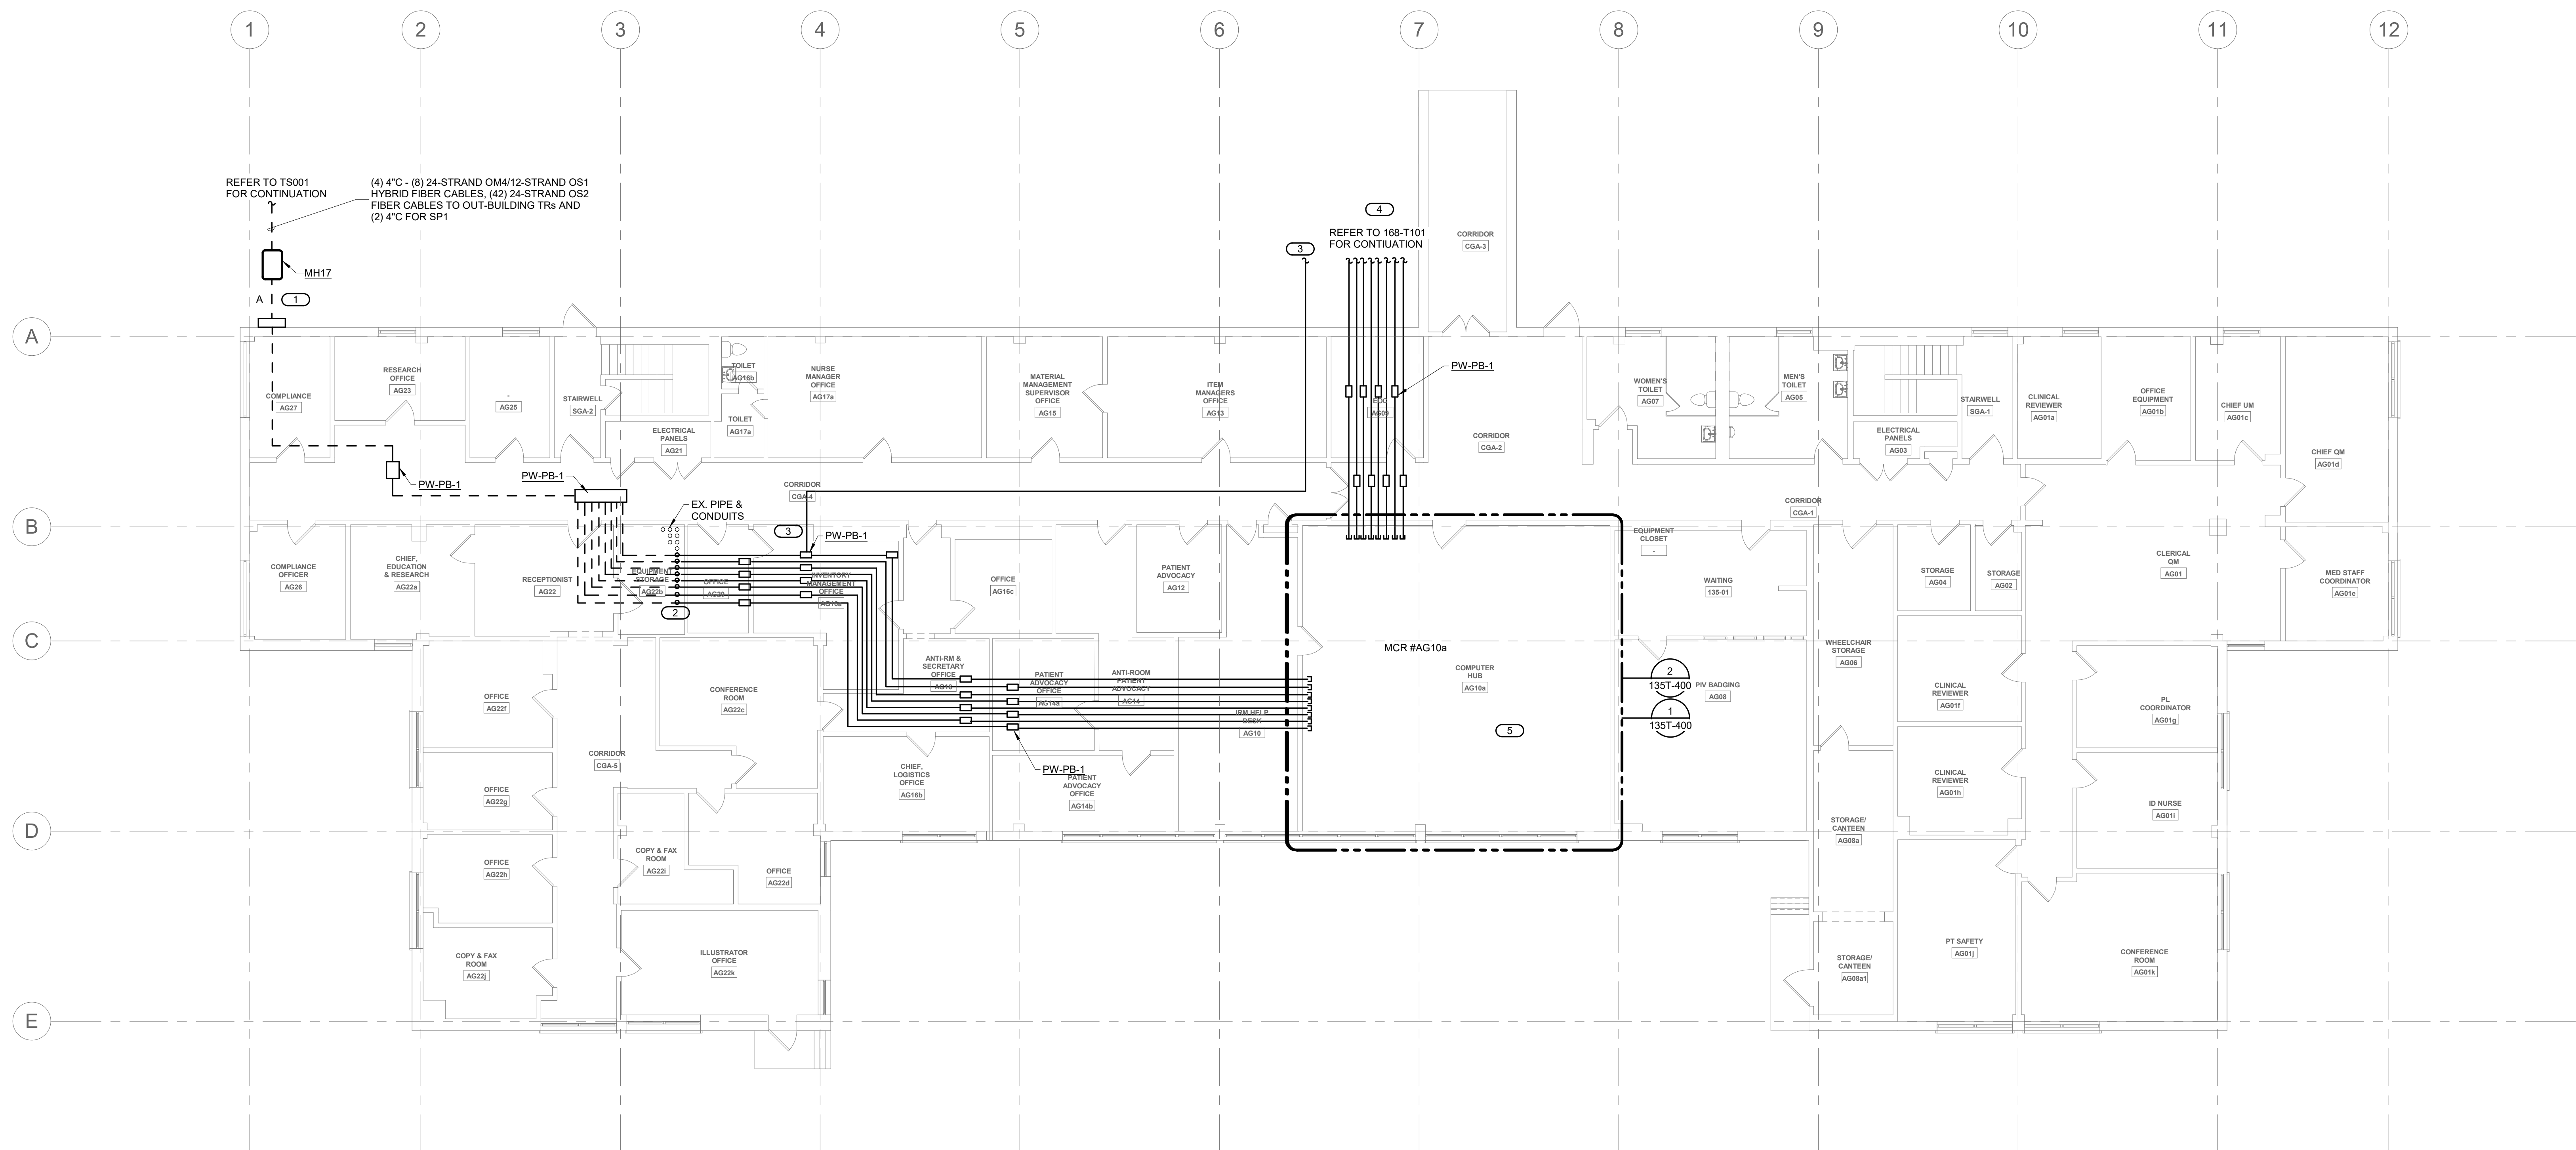


1 LEVEL 00 - GROUND PLAN - TECHNOLOGY
1/8" = 1'-0"

		CONSULTANT	ARCHITECT/ENGINEER OF RECORD	STAMP	Office of Construction and Facilities Management	Drawing Title	Phase	Project Title	Project Number		
		ENGINEERING DISCIPLINE:	A/E:	REGISTERED COMMUNICATIONS DISTRIBUTION ENGINEER  Eddie C. Wiles, Jr. Res. No. 191560R Expires 12-31-2025 RCDD		BLDG. 135 LEVEL 00 - GROUND PLAN	100% CONSTRUCTION DOCUMENTS	EHRM INFRASTRUCTURE UPGRADES - HAMPTON	509-222-700		
		 www.imegcorp.com 225 W WASHINGTON STREET SUITE 2700 CHICAGO, IL 60608 P-312.294.0501 F-312.294.0003 PROJECT #22010109.00	SPEES DESIGN BUILD 23830 PACIFIC HIGHWAY S. SUITE 203 KENT, WA 98032			-TECHNOLOGY		Building Number 135			
			 SPEESDESIGNBUILD			Approved:	FULLY SPRINKLERED	Location HAMPTON VA MEDICAL CENTER, HAMPTON, VIRGINIA	Drawing Number		
								Issue Date 05/09/2025	Checked EW	Drawn IMEG	135T-200
											691 of 713
Revisions:	Date:				VA U.S. Department of Veterans Affairs						

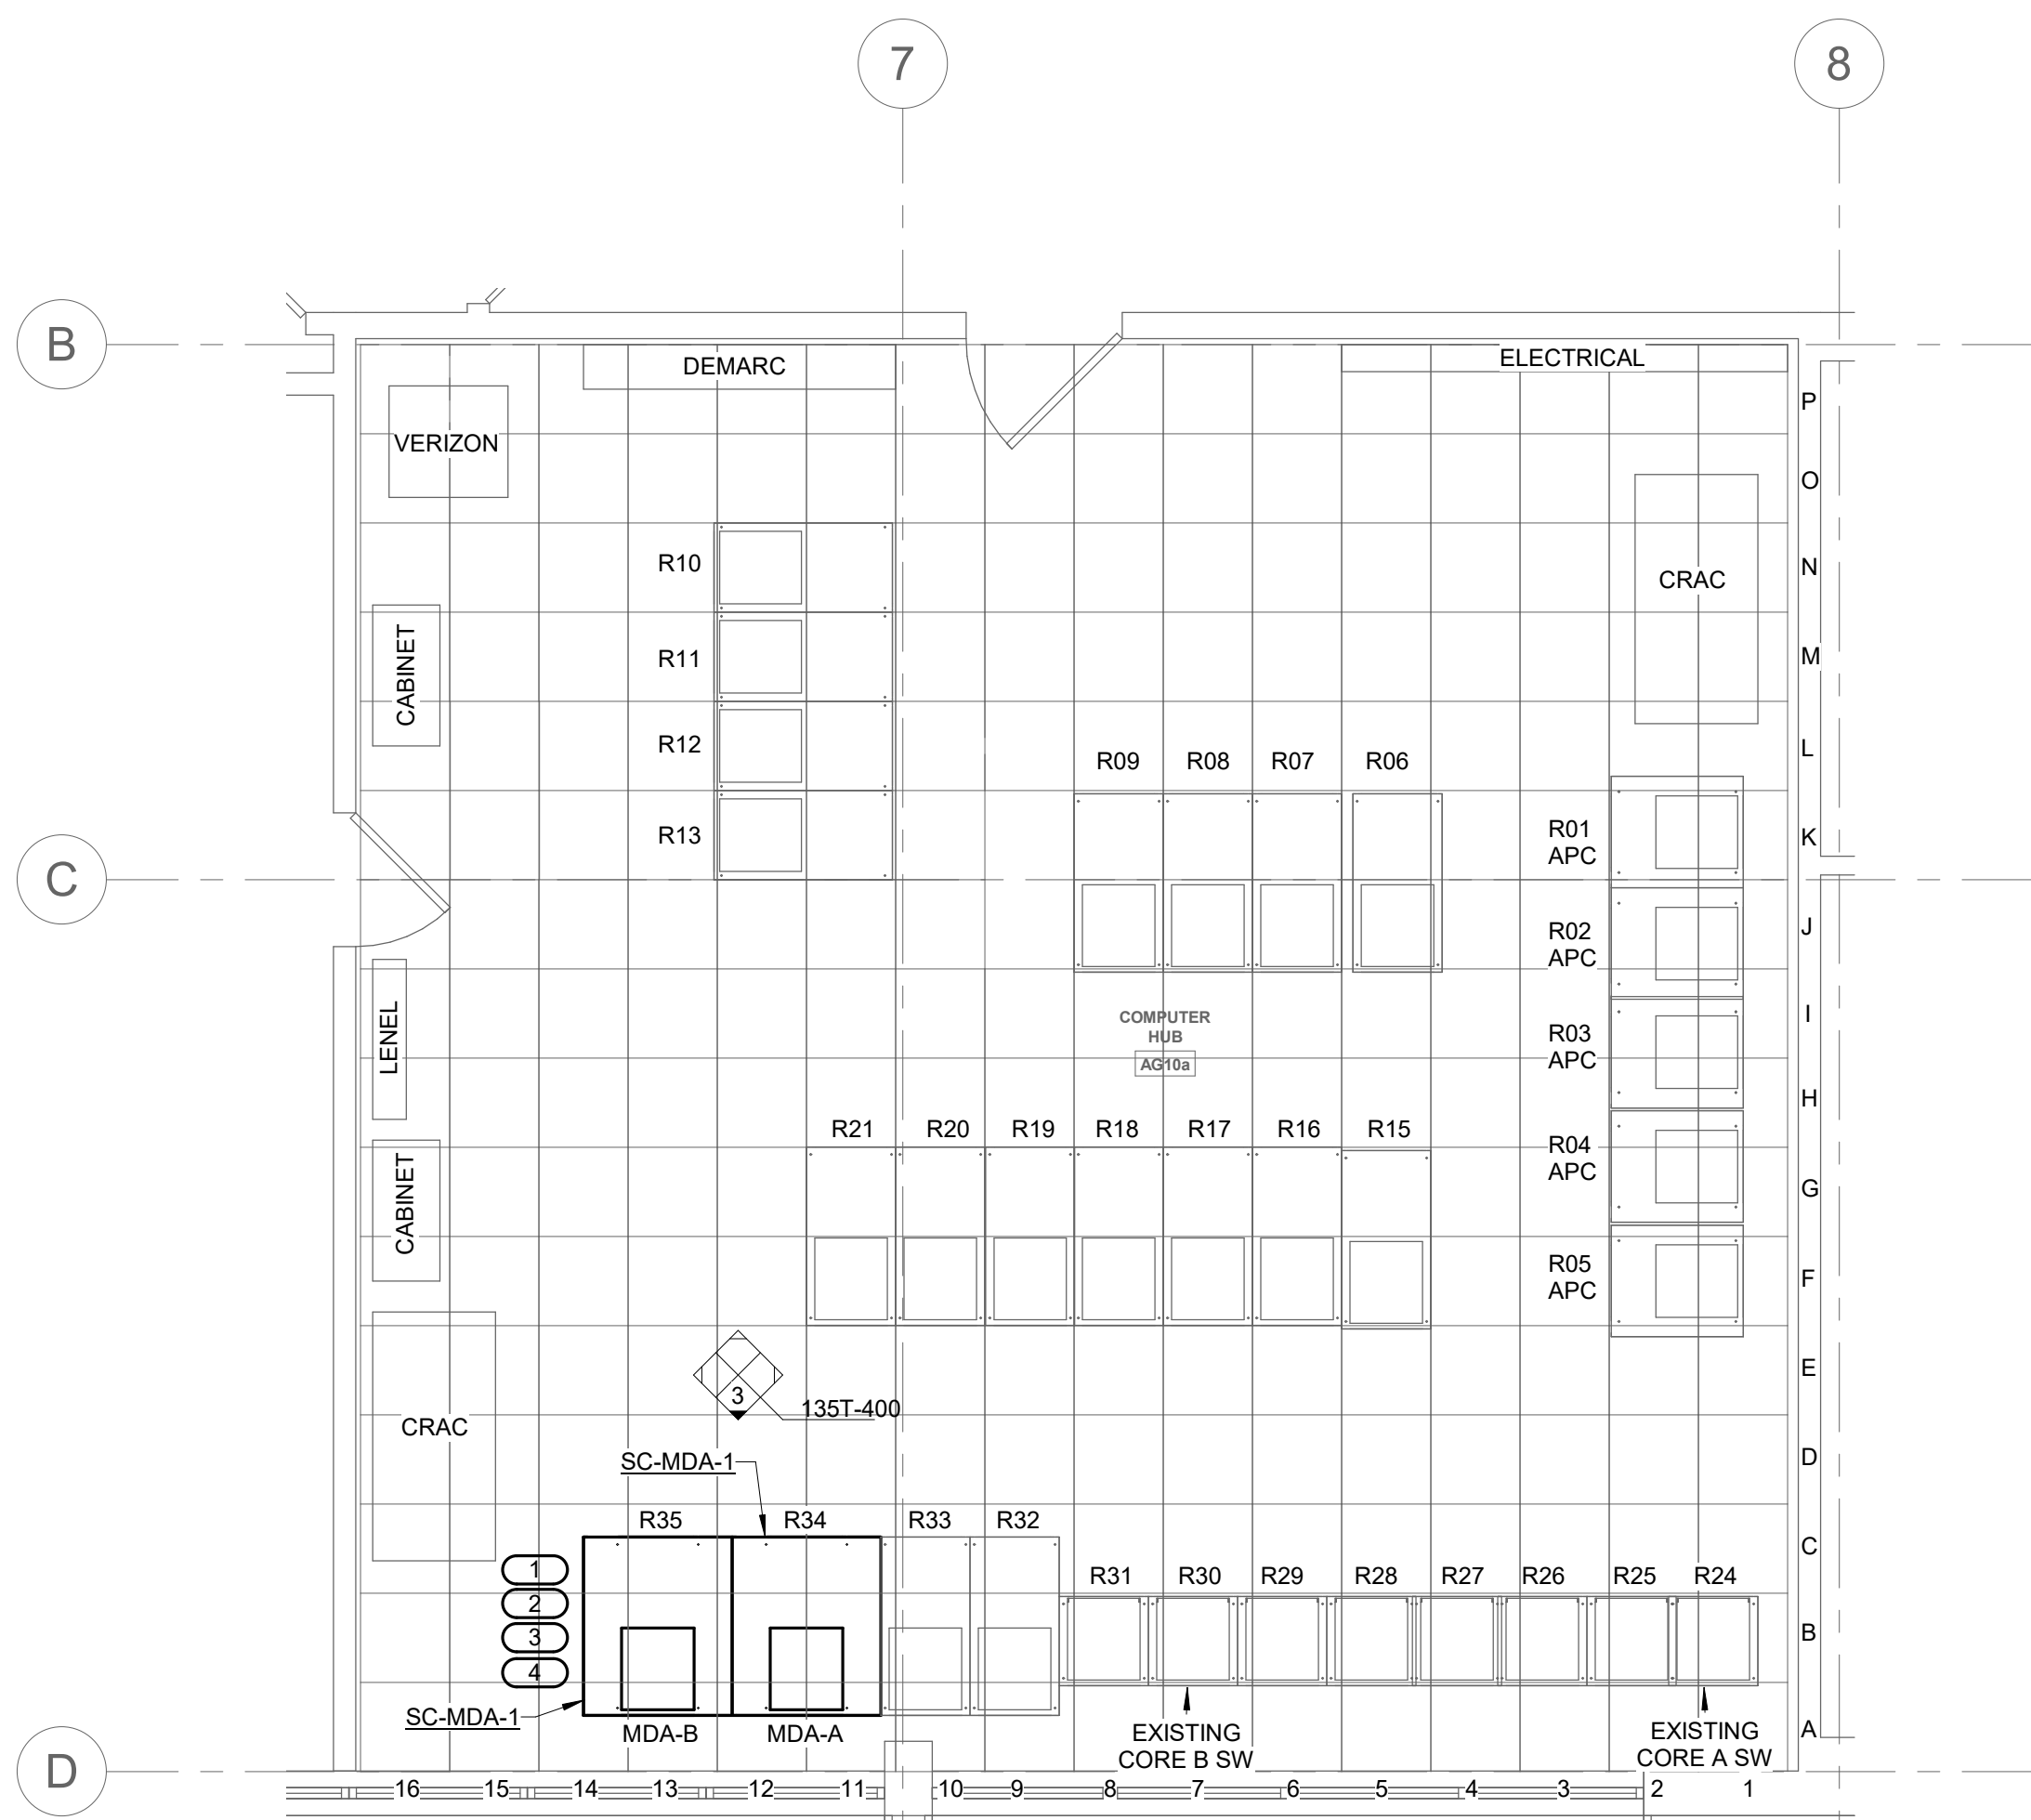


1 EXISTING MCR #AG10 ENLARGEMENT

- KEYNOTES: #
1. PROVIDE NEW NETWORK CABINETS IN EXISTING MAIN COMPUTER ROOM #AG10. PROVIDE FIBER DISTRIBUTION HOUSINGS AND FIBER CASSETTES IN NETWORK CABINET TO TERMINATE NEW FIBER BACKBONE CABLES FROM EACH TR. FIELD TERMINATE TR FIBER CABLES AT BOTH ENDS WITH LC CONNECTORS.
 2. PROVIDE FIBER PATCH CABLES FOR ALL TR FIBER BACKBONE CABLES FROM FIBER DISTRIBUTION HOUSINGS TO DESIGNATED CORE SWITCH. FIBER PATCH CABLES AND STRUCTURED CABLING WITHIN THE EXISTING MCR SHALL BE FURNISHED WITH FACTORY PRE-TERMINATED CONNECTORS.
 3. THE PATCHING EQUIPMENT IN THE NEW NETWORK CABINET SHALL BE FRONT MOUNTED.
 4. NEW BACKBONE CABLING FOR EACH NEW/RE-USED TR SHALL BE PATCHED OVER TO EXISTING CORE SWITCHES, ONE TR AT A TIME, AND SHALL BE PHASED FOR CORE A AND CORE B. NEW CORE A FIBER SHALL BE TERMINATED, TESTED AND ACTIVATED WHILE EXISTING CORE B FIBER FOR SAME TR REMAINS ACTIVE. AFTER NEW CORE A FIBER IS PATCHED OVER TO CORE A SWITCH, NEW CORE B FIBER SHALL BE TERMINATED, TESTED AND PATCHED OVER TO EXISTING CORE B SWITCH. TYPICAL SEQUENCE FOR EACH TR.

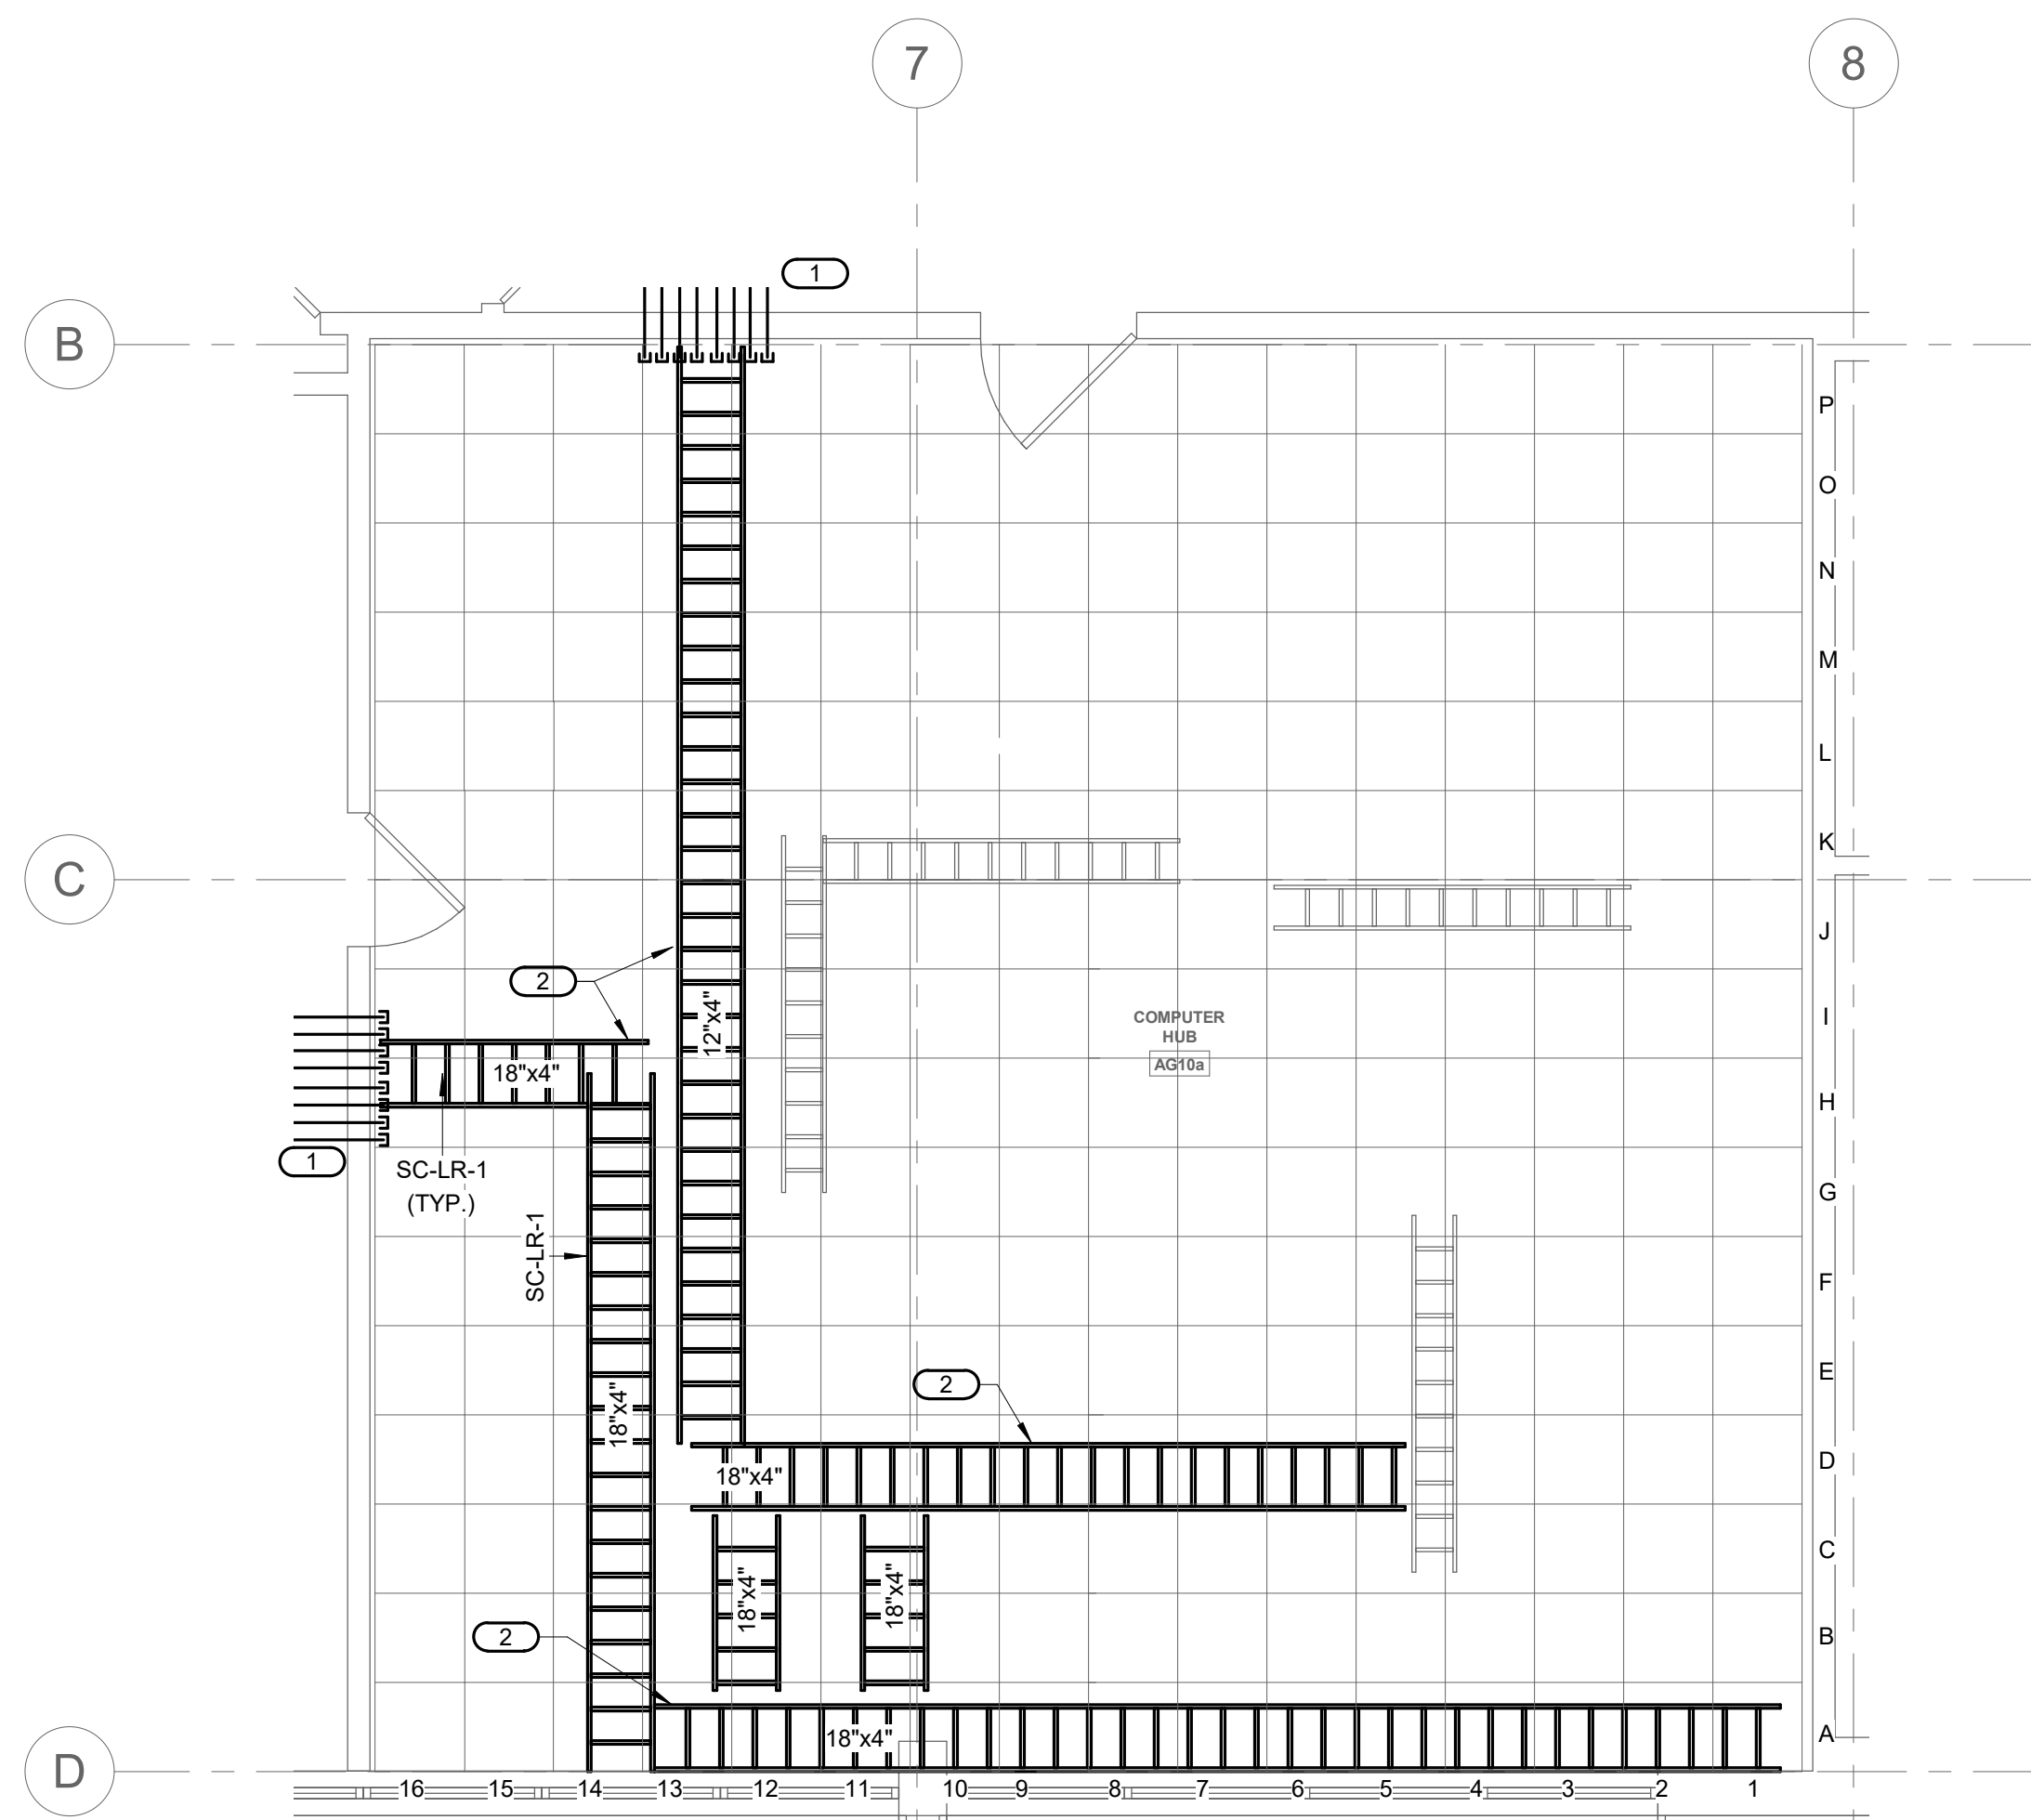

2 EXISTING MCR #AG10 PATHWAYS

- KEYNOTES: #
1. PROVIDE PENETRATION THRU WALLS OF EXISTING MCR #AG10a AND STUB FIBER BACKBONE AND SERVICE PROVIDER CONDUITS INTO ROOM AT HEIGHT ABOVE EXISTING LADDER RUNWAYS.
 2. PROVIDE NEW 18"W LADDER RUNWAYS AT LOCATIONS INDICATED WITH WATERFALL CABLE DROP SUPPORTS ABOVE NEW SERVER CABINETS. INSTALL NEW LADDER RUNWAYS AT SAME HEIGHT OF EXISTING LADDER RUNWAYS. ADJUST LOCATION, AS NECESSARY, TO AVOID INTERFERENCE WITH LIGHTING FIXTURES, EQUIPMENT AND PIPING. CONTINUE ROUTE OF NEW FIBER CABLES ON LADDER RUNWAYS TO NEW CORE A AND CORE B SERVER CABINETS.

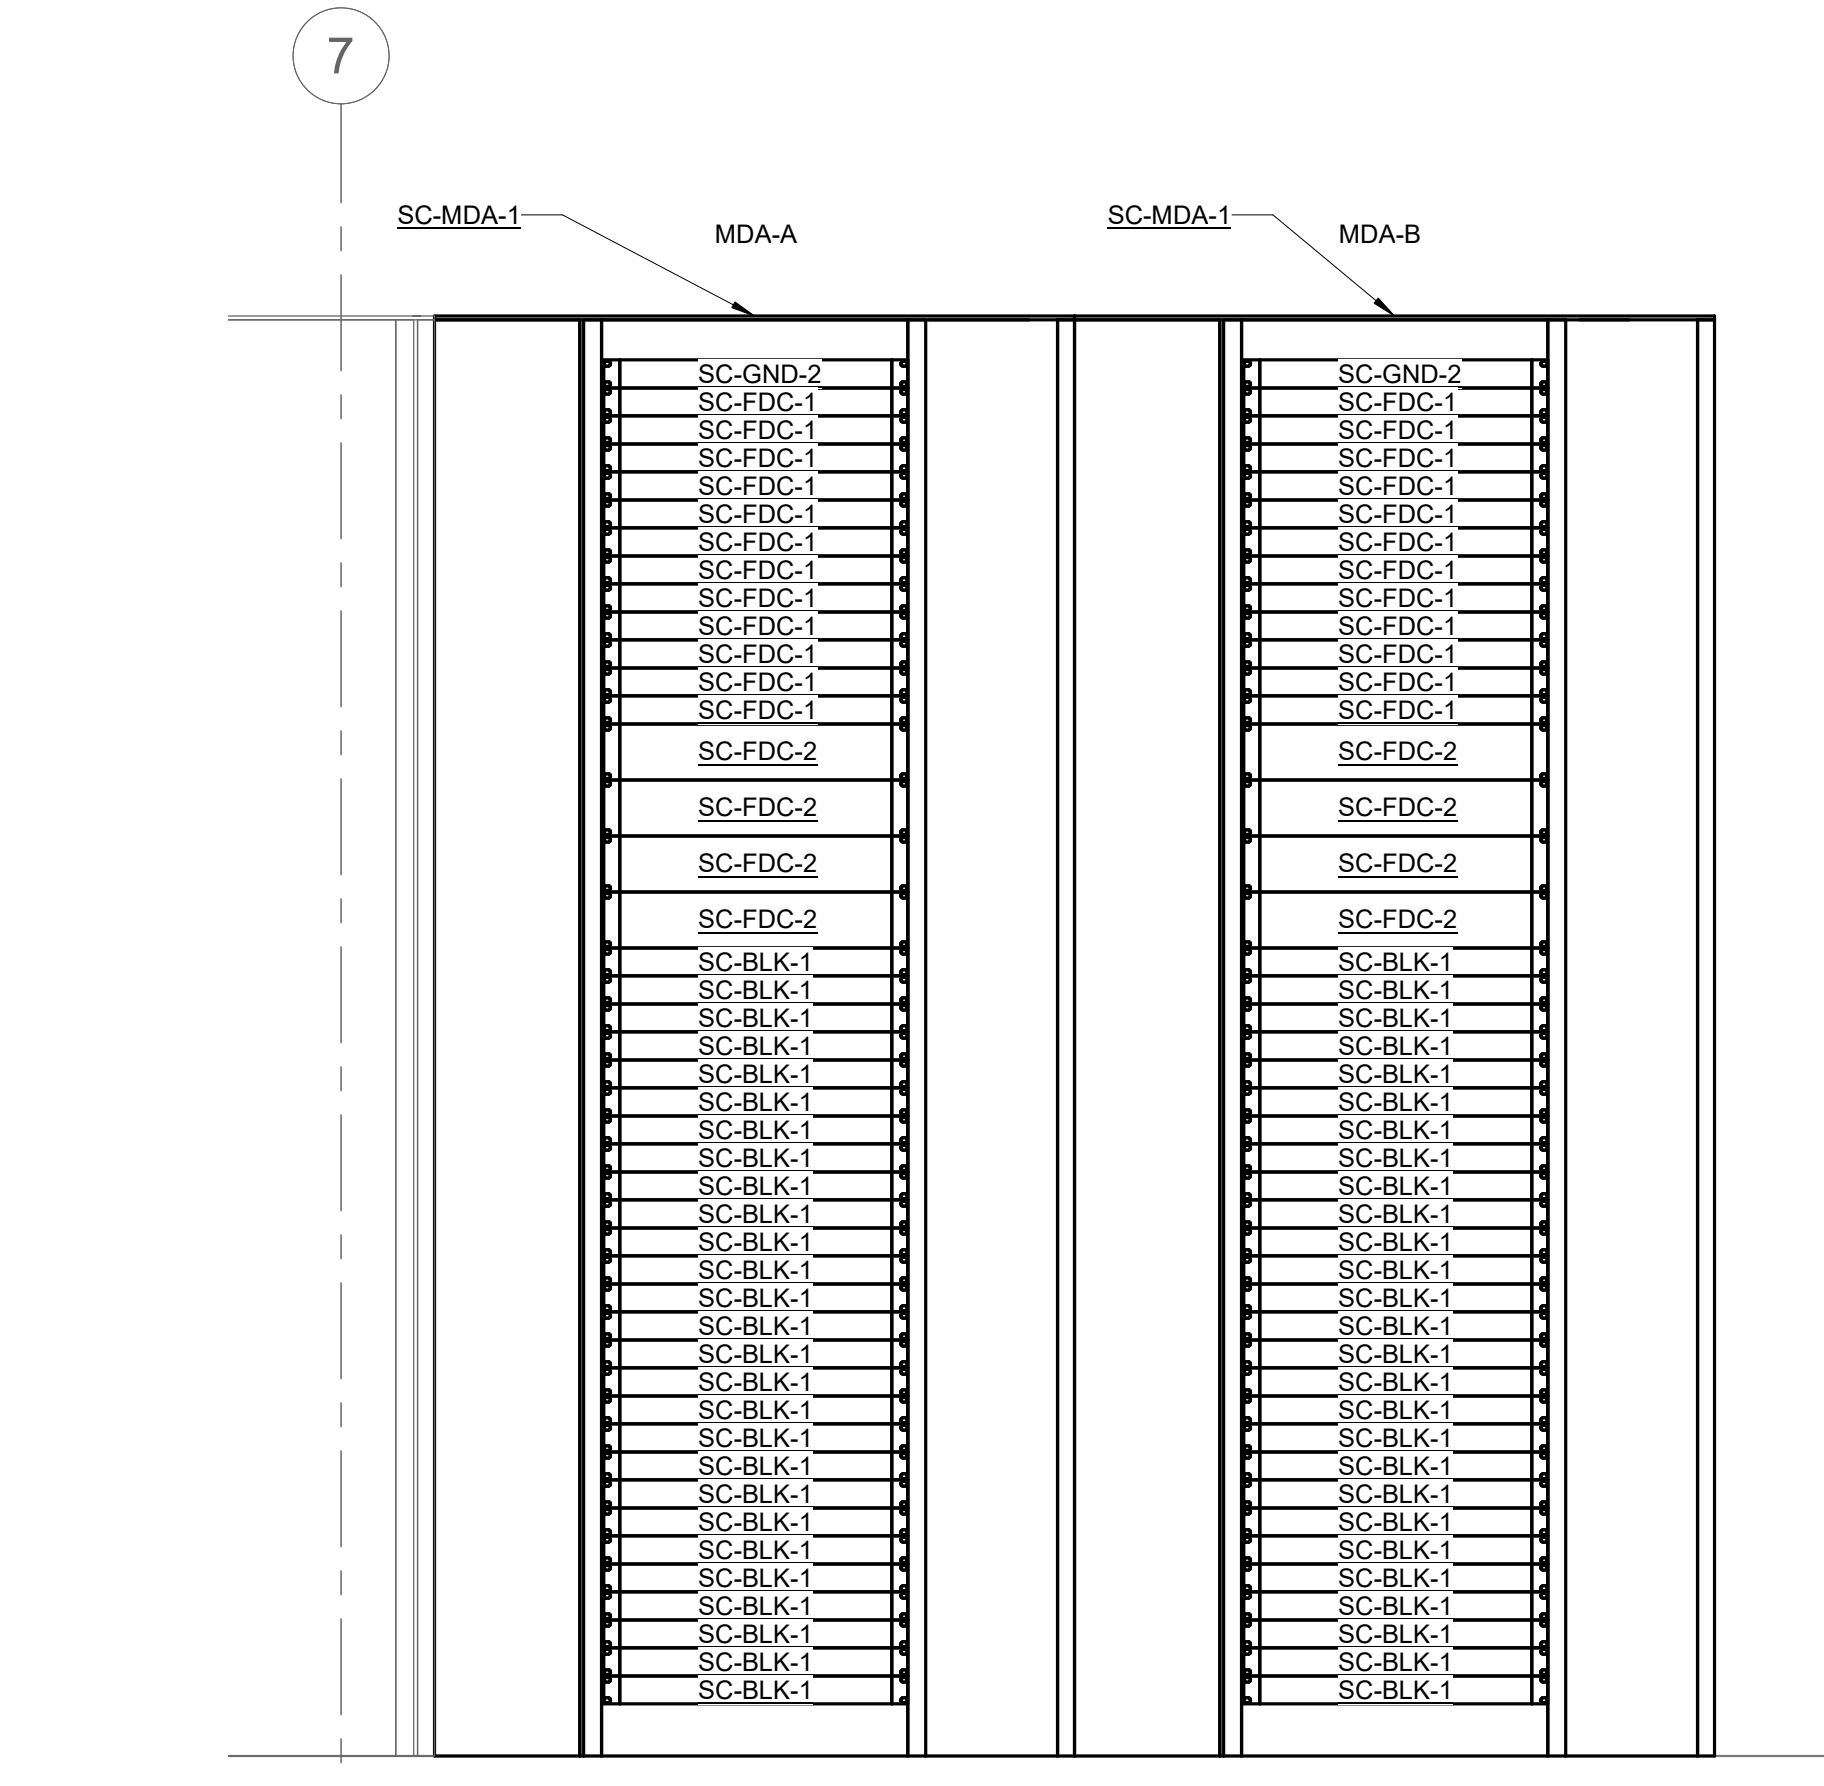

3 NEW MDA-A AND MDA-B CABINET ELEVATIONS

BM 360/509/22-700 Validation EHRM360-509-01-05_T_021.rvt 8/2/2025 8:06:57 AM	
---	--	--	

- SHEET NOTES:
1.

REFER TO SITE PLAN TS001 FOR ADDITIONAL INFORMATION.
2.

REFER TO TS00 AND TS01 FOR CAMPUS OPTICAL FIBER CABLE RISER DIAGRAMS.
3.

REFER TO 271400 FOR HANDHOLE DETAIL.
4.


NEW BACKBONE OPTICAL FIBER CABLES SHALL BE INDOOR/OUTDOOR TYPE.
5.

ALL BACKBONE OPTICAL FIBER CABLE PATHWAYS SHALL BE NEW. DO NOT RE-USE EXISTING BACKBONE CABLE PATHWAYS FOR NEW BACKBONE CABLES.
6.



TRANSITION PVC CONDUITS TO GRC IN CRAWL SPACE OR EXPOSED EXTERIOR LOCATIONS. TRANSITION TO EMT CONDUITS AT INTERIOR OF BUILDING. SEAL ALL PENETRATIONS TO MAINTAIN FIRE-RATINGS OF WALL, CEILING AND FLOORS. SEAL ALL PENETRATIONS TO MAINTAIN FIRE-RATINGS OF WALL, CEILING AND FLOORS.
- KEY NOTES:

#
1.


PROVIDE PULLBOX ON EXTERIOR WALL AT HEIGHT ABOVE FINISHED CEILING. ROUTE CONDUIT UP WALL INTO PULLBOX. PROVIDE PENETRATION THRU WALL AND ROUTE CONDUIT THRU WALL AND ABOVE CORRIDOR CEILING INTO TR #1C103C, TR #A125, AND TR #B105B.

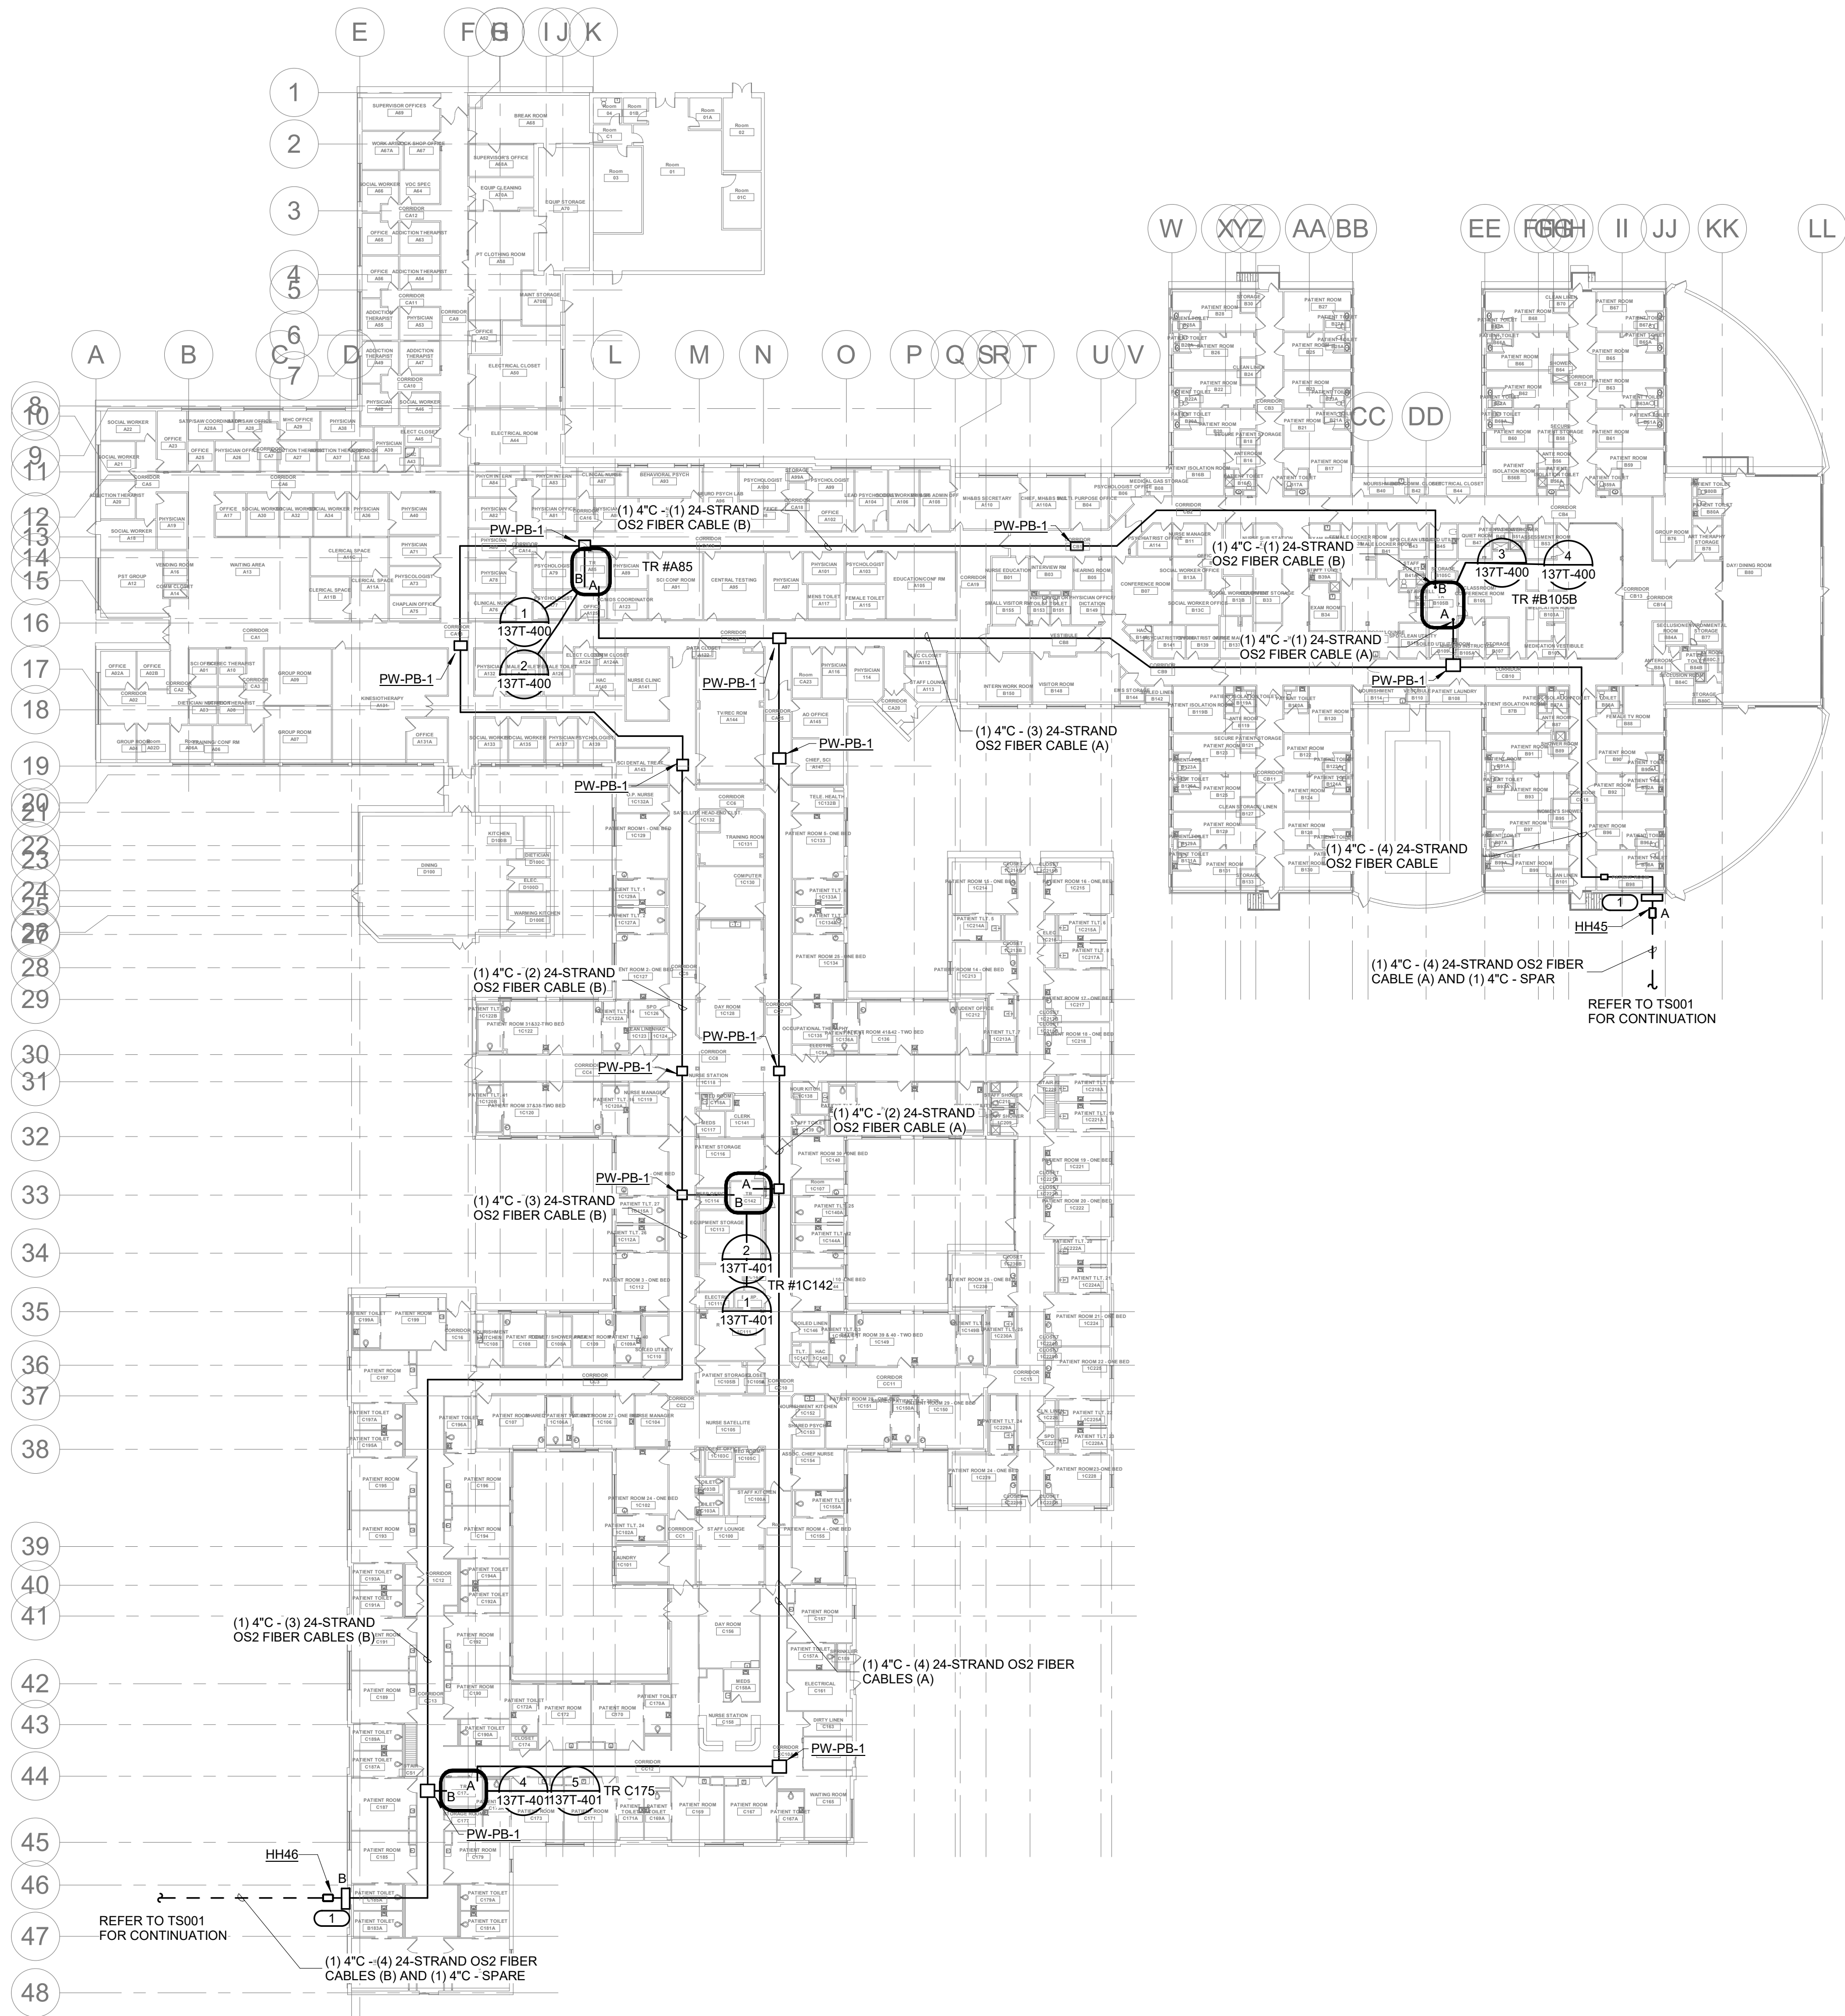


1 **LEVEL 01 PLAN - TECHNOLOGY**
1" = 30'-0"

 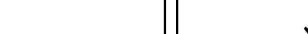		CONSULTANT	ARCHITECT/ENGINEER OF RECORD	STAMP	Office of Construction and Facilities Management	Drawing Title	Phase	Project Title	Project Number		
		ENGINEERING DISCIPLINE:	A/E:	 RCDD		BLDG.137 LEVEL 01 PLAN - TECHNOLOGY	100% CONSTRUCTION DOCUMENTS	EHRM INFRASTRUCTURE UPGRADES - HAMPTON	509-22-700		
		 www.imegcorp.com 225 W WASHINGTON STREET SUITE 2700 CHICAGO, IL 60606 P: 312.294.0501 F: 312.294.0003 PROJECT #22010109.00	23830 PACIFIC HIGHWAY S. SUITE 203 KENT, WA 98032			 SPEEDSDSIGNBUILD	Approved:	FULLY SPRINKLERED	Location	Building Number	
								HAMPTON VA MEDICAL CENTER, HAMPTON, VIRGINIA	137		
Revisions:	Date:				 U.S. Department of Veterans Affairs			Issue Date	Checked	Drawn	Drawing Number
								05/09/2025	EW	IMEG	137T-201
											693 of 713


A
B
C
D
E
F

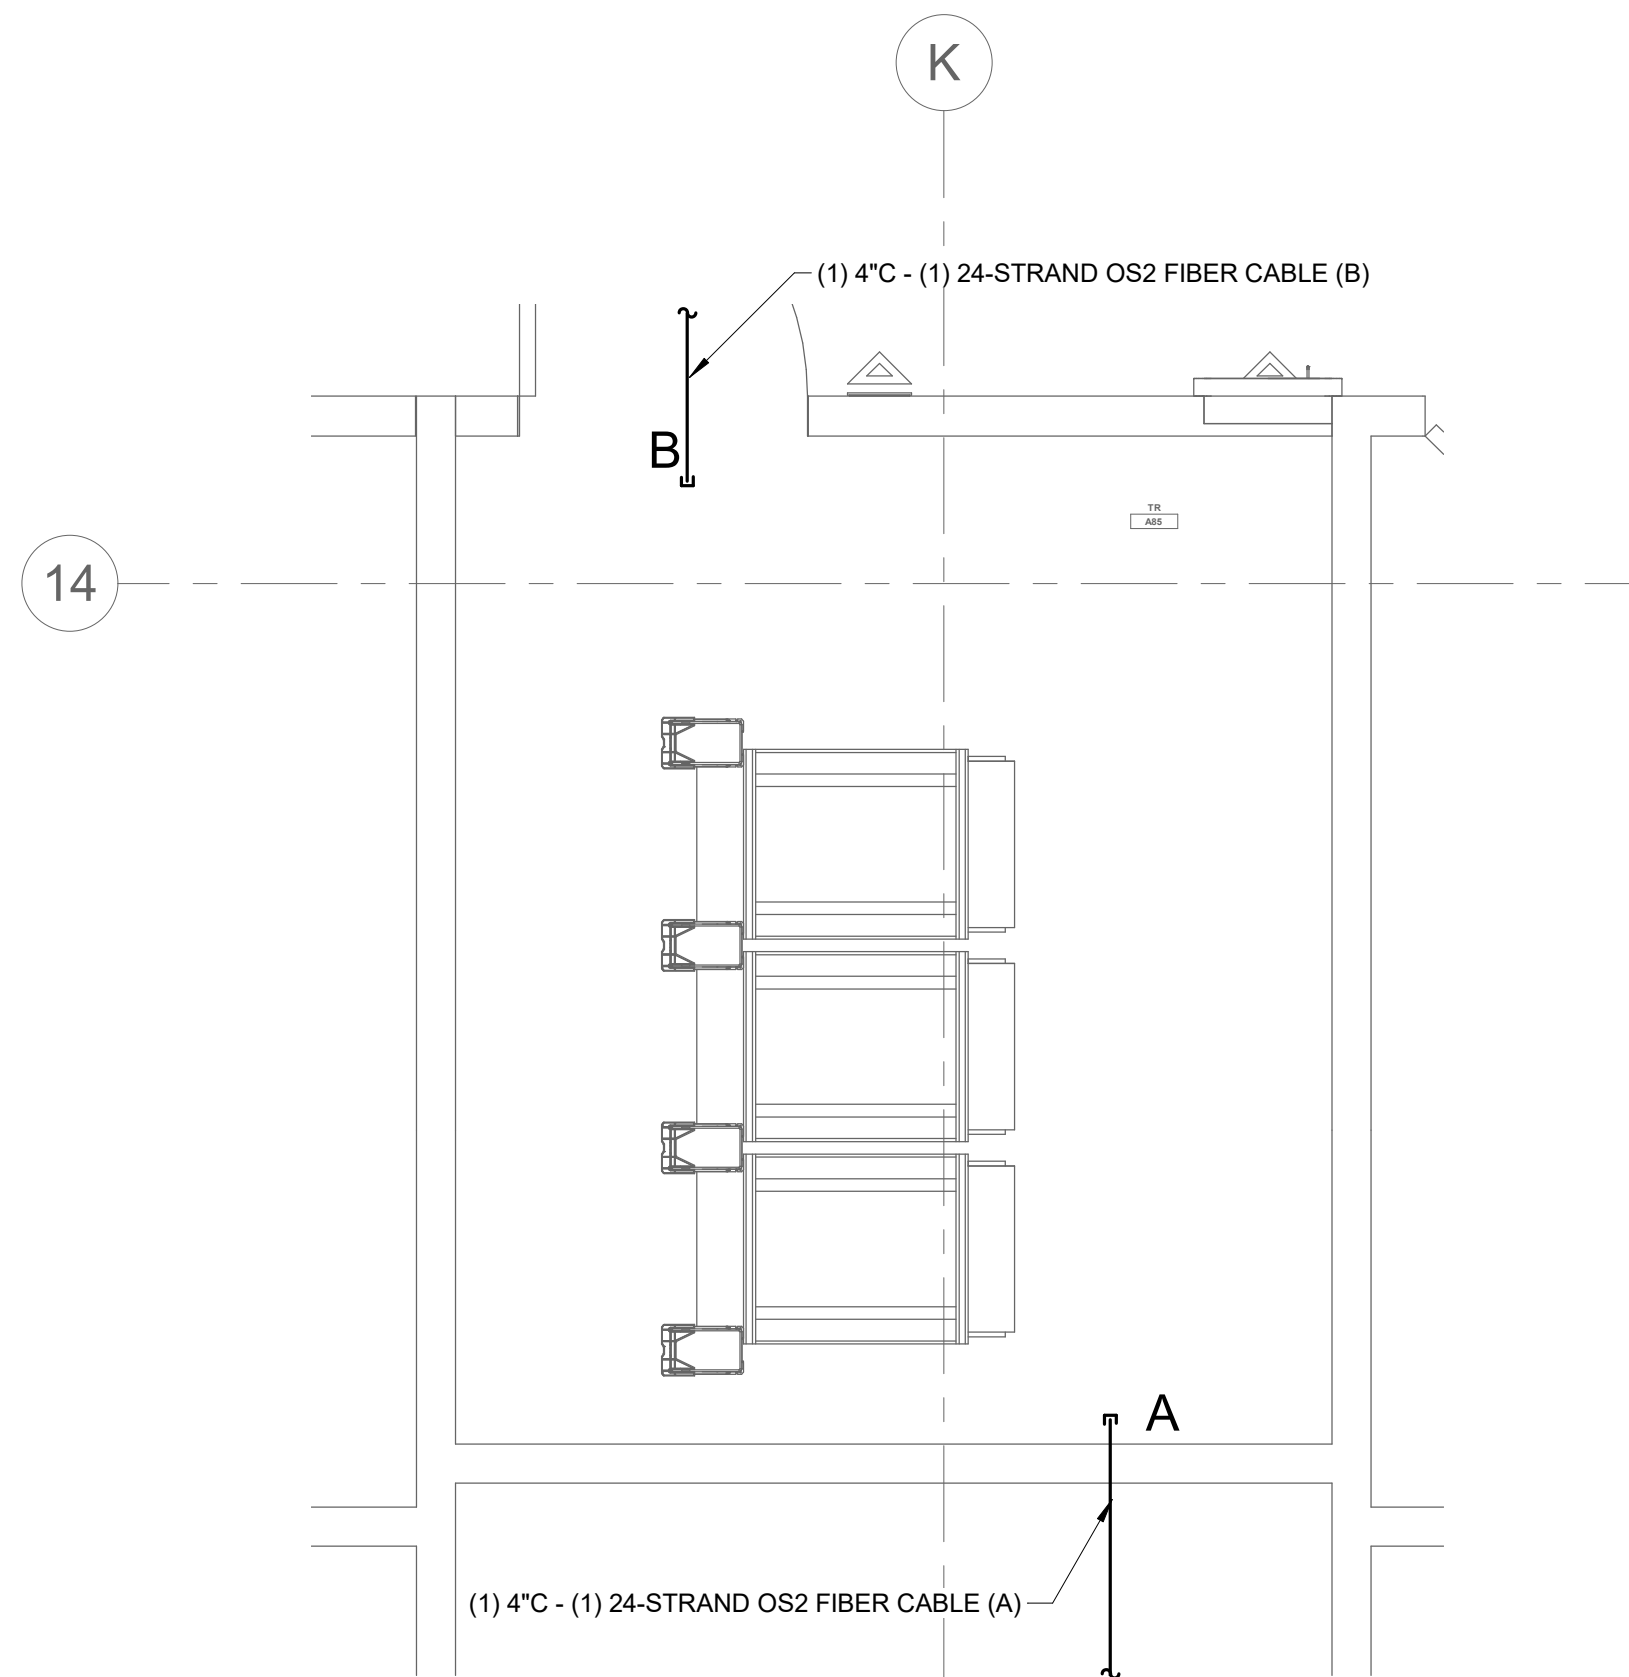


1 TELECOM ROOM ENLARGEMENT PLAN TR #A85
1/2" = 1'-0"
NOTES:
1. REFER TO ELECTRICAL DRAWINGS FOR ROOM LAYOUT AND RACK ELEVATIONS.
2. ROUTE OPTICAL FIBER CABLE TO OVERHEAD CABLE TRAY AND TERMINATE IN FIBER DISTRIBUTION CABINET.
KEYNOTES: (#)
1. THROUGH WALL PENETRATION FOR BACKBONE CONDUIT. OPTICAL FIBER CABLE CONTINUES ON CABLE TRAY TO RACKS.

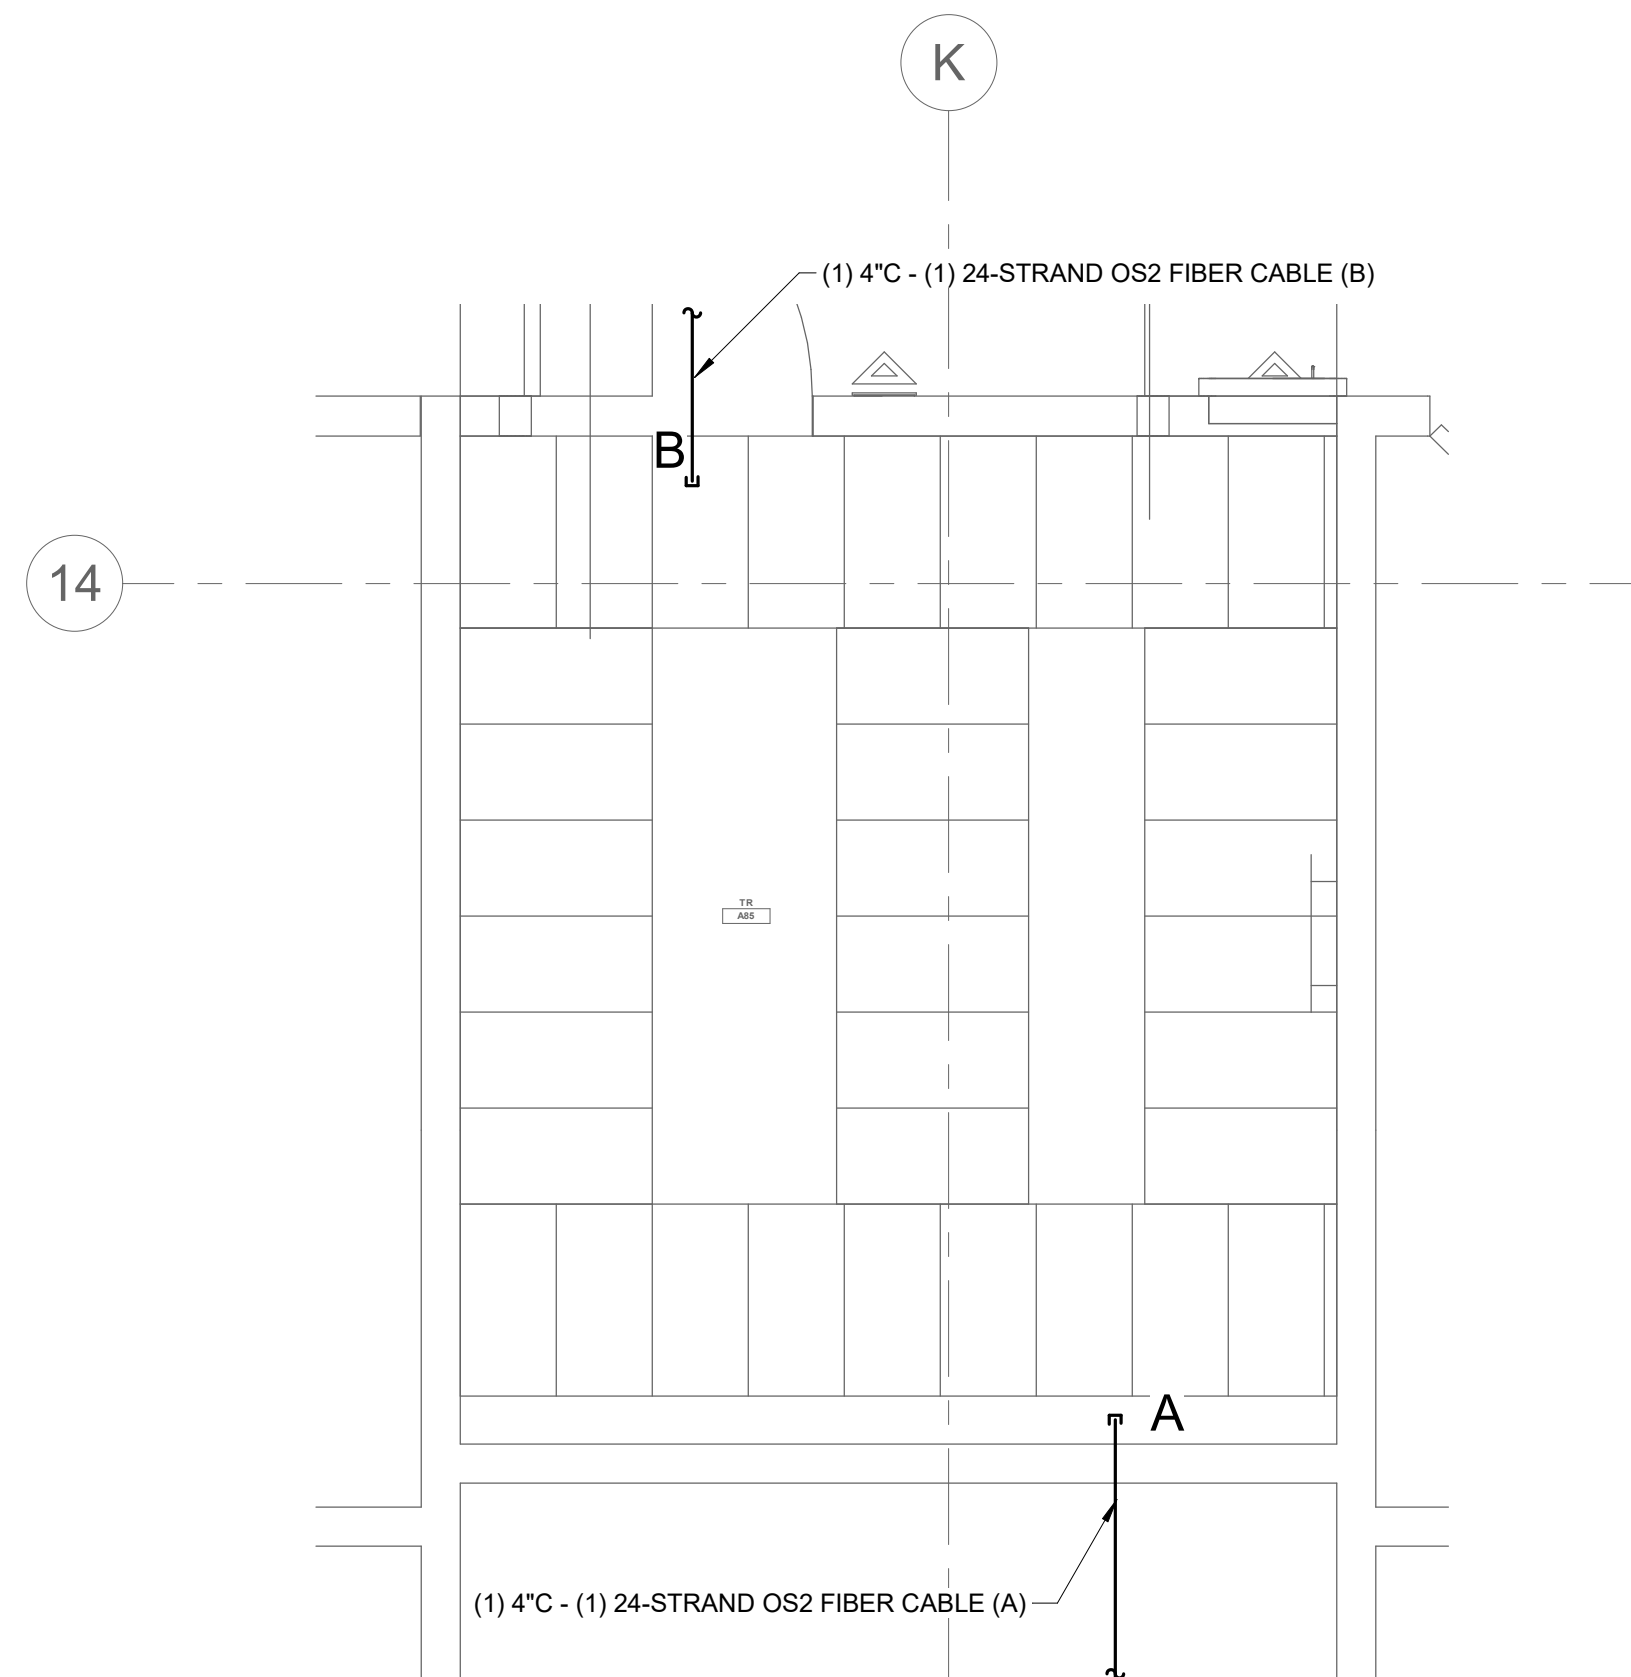

2 TELECOM ROOM PATHWAY PLAN TR #A85
1/2" = 1'-0"

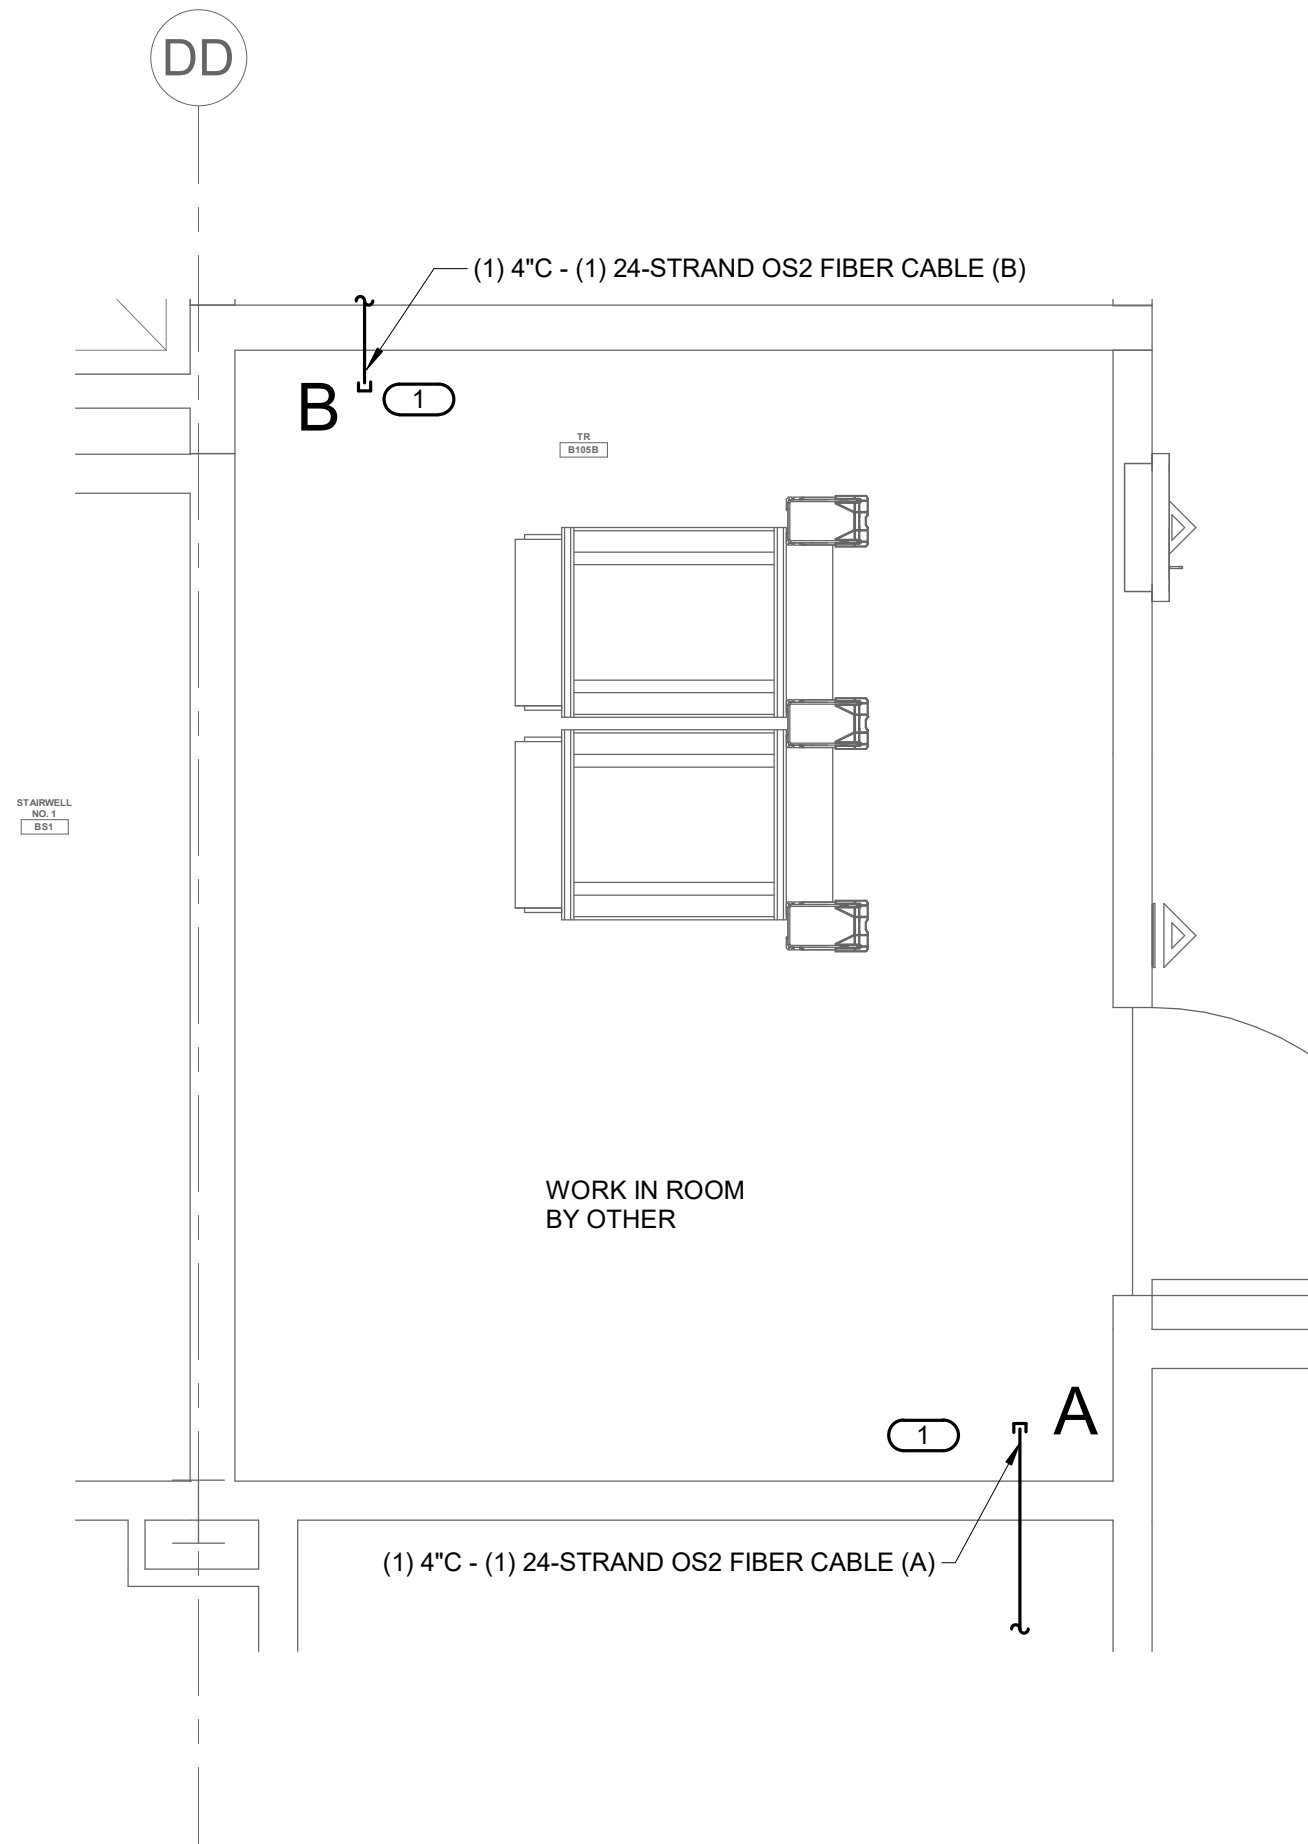

3 TELECOM ROOM ENLARGEMENT PLAN - TR #B105B
1/2" = 1'-0"
NOTES:
1. REFER TO ELECTRICAL DRAWINGS FOR ROOM LAYOUT AND RACK ELEVATIONS.
2. ROUTE OPTICAL FIBER CABLE TO OVERHEAD CABLE TRAY AND TERMINATE IN FIBER DISTRIBUTION CABINET.
KEYNOTES: (#)
1. THROUGH WALL PENETRATION FOR BACKBONE CONDUIT. OPTICAL FIBER CABLE CONTINUES ON CABLE TRAY TO RACKS.

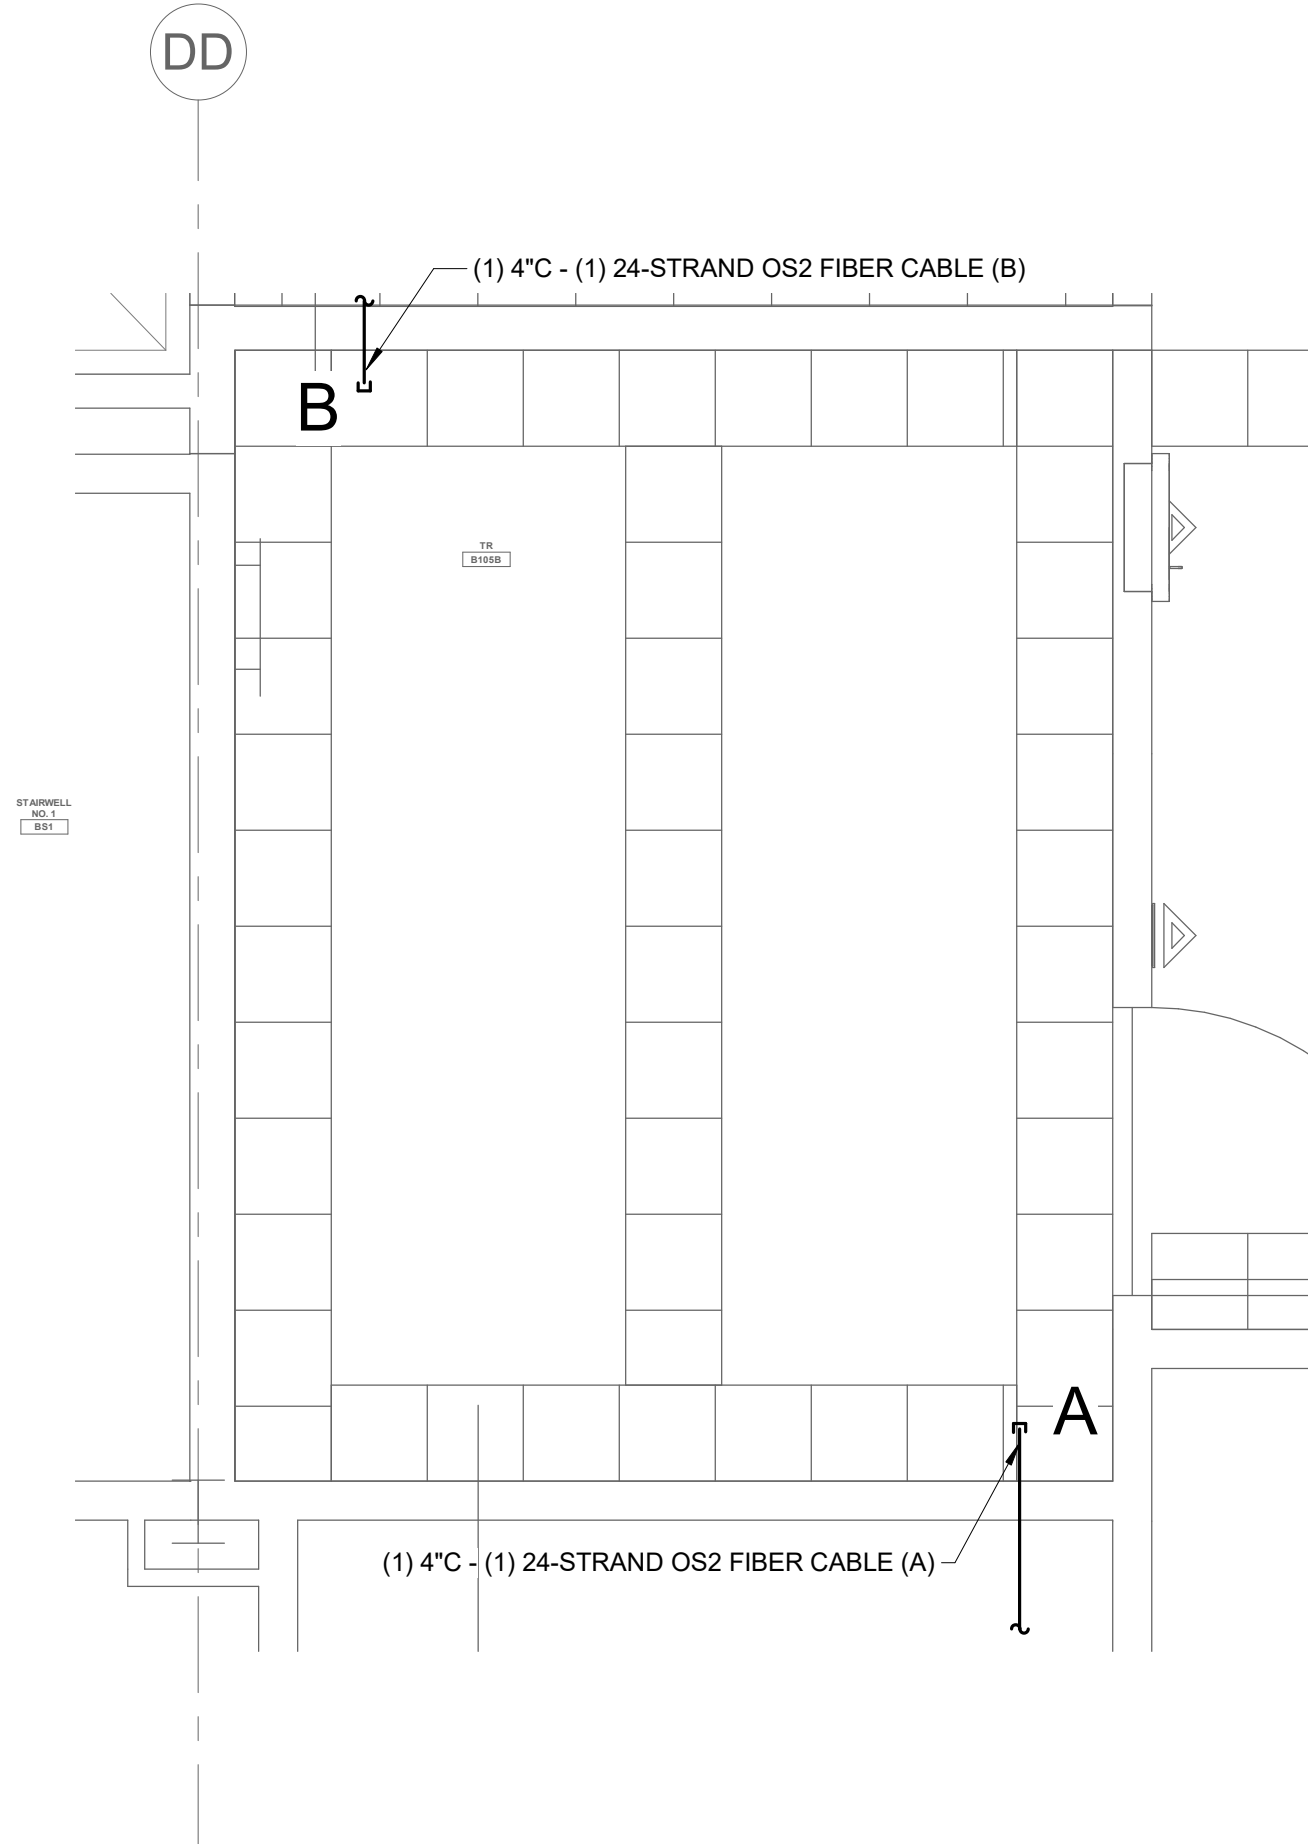

4 TELECOM ROOM PATHWAY PLAN - TR #B105B
1/2" = 1'-0"

BVA 360/509-22-700
VA Hampton
EHRM 509-22-700 B137.T_R01.rvt

8/13/2025 11:45:10 AM

Revisions:	Date:

CONSULTANT

ENGINEERING DISCIPLINE:

IMEG

225 W WASHINGTON STREET
SUITE 2700
CHICAGO, IL 60606
P: 312.294.0501 F: 312.294.0003
PROJECT #22010109.00

ARCHITECT/ENGINEER OF RECORD

A/E:

SPEES DESIGN BUILD
23830 PACIFIC HIGHWAY S. SUITE 203
KENT, WA 98032

SDB SPEESDESIGNBUILD

STAMP

REGISTERED COMMUNICATIONS DISTRIBUTION DESIGNER

Bicsi

ES&C No. 1919026
EXPIRES 03-01-2025

RCCD

Office of
Construction
and Facilities
Management

VA U.S. Department
of Veterans Affairs

Drawing Title

BLDG.137 TECHNOLOGY ENLARGED PLANS

Approved:

Phase

100% CONSTRUCTION
DOCUMENTS

FULLY SPRINKLERED

Project Title

EHRM INFRASTRUCTURE
UPGRADES - HAMPTON

Location

HAMPTON VA MEDICAL CENTER, HAMPTON, VIRGINIA

Issue Date

05/09/2025

Checked

EW

Drawn

IMEG

Project Number

509-22-700

Building Number

137

Drawing Number

137T-400

694 of 713

A

B

C

D

E

F

A


B

C


D

E


F

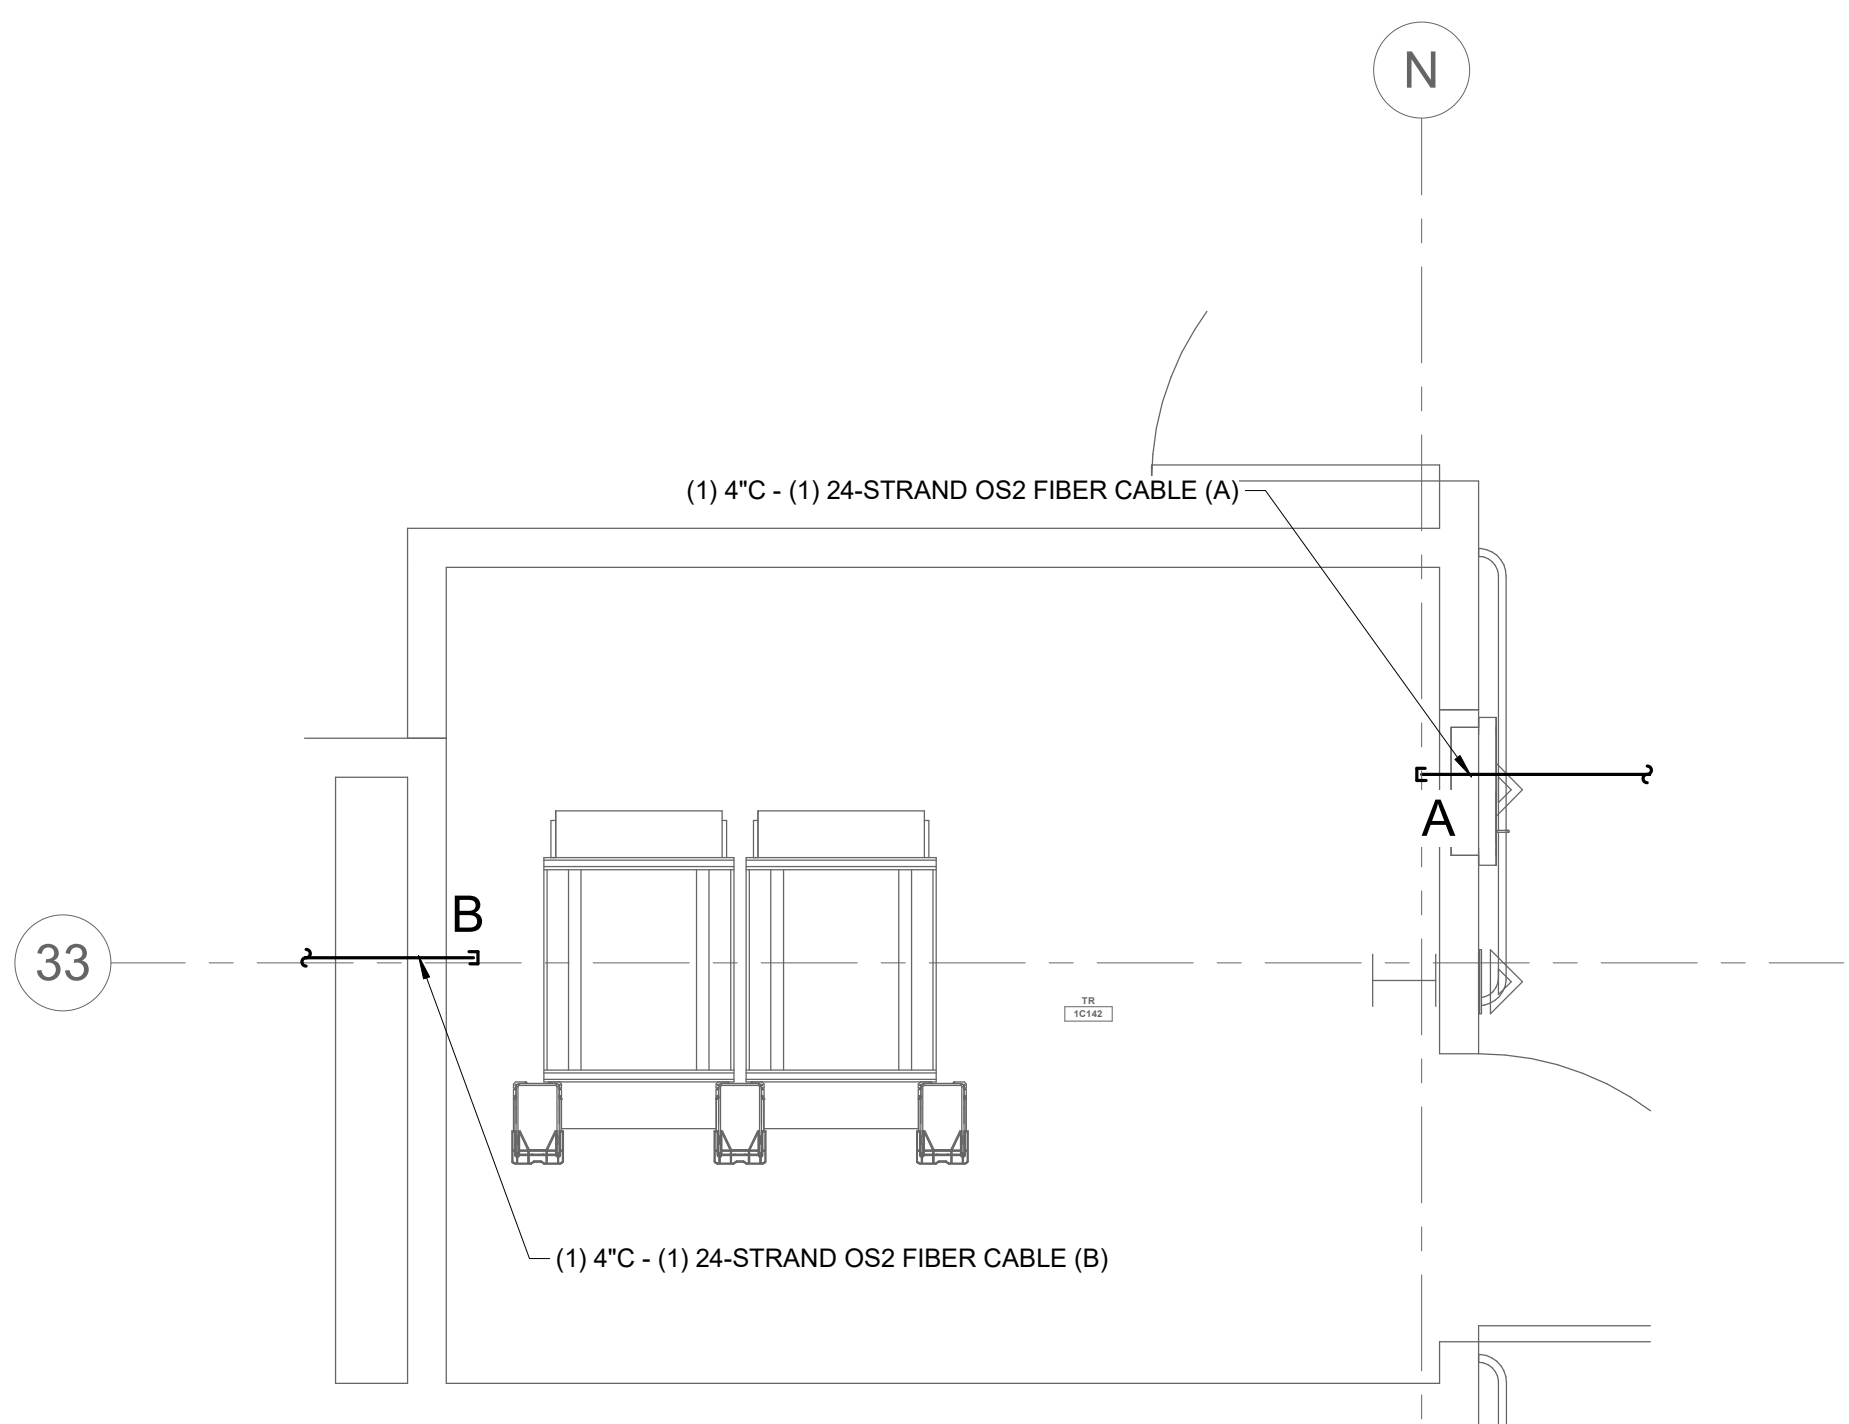


1 TELECOM ROOM ENLARGEMENT PLAN TR #1C142
1/2" = 1'-0"
NOTES:
1. REFER TO ELECTRICAL DRAWINGS FOR ROOM LAYOUT AND RACK ELEVATIONS.
2. ROUTE OPTICAL FIBER CABLE TO OVERHEAD CABLE TRAY AND TERMINATE IN FIBER DISTRIBUTION CABINET.
KEYNOTES: **C** #
1. THROUGH WALL PENETRATION FOR BACKBONE CONDUIT. OPTICAL FIBER CABLE CONTINUES ON CABLE TRAY TO RACKS.

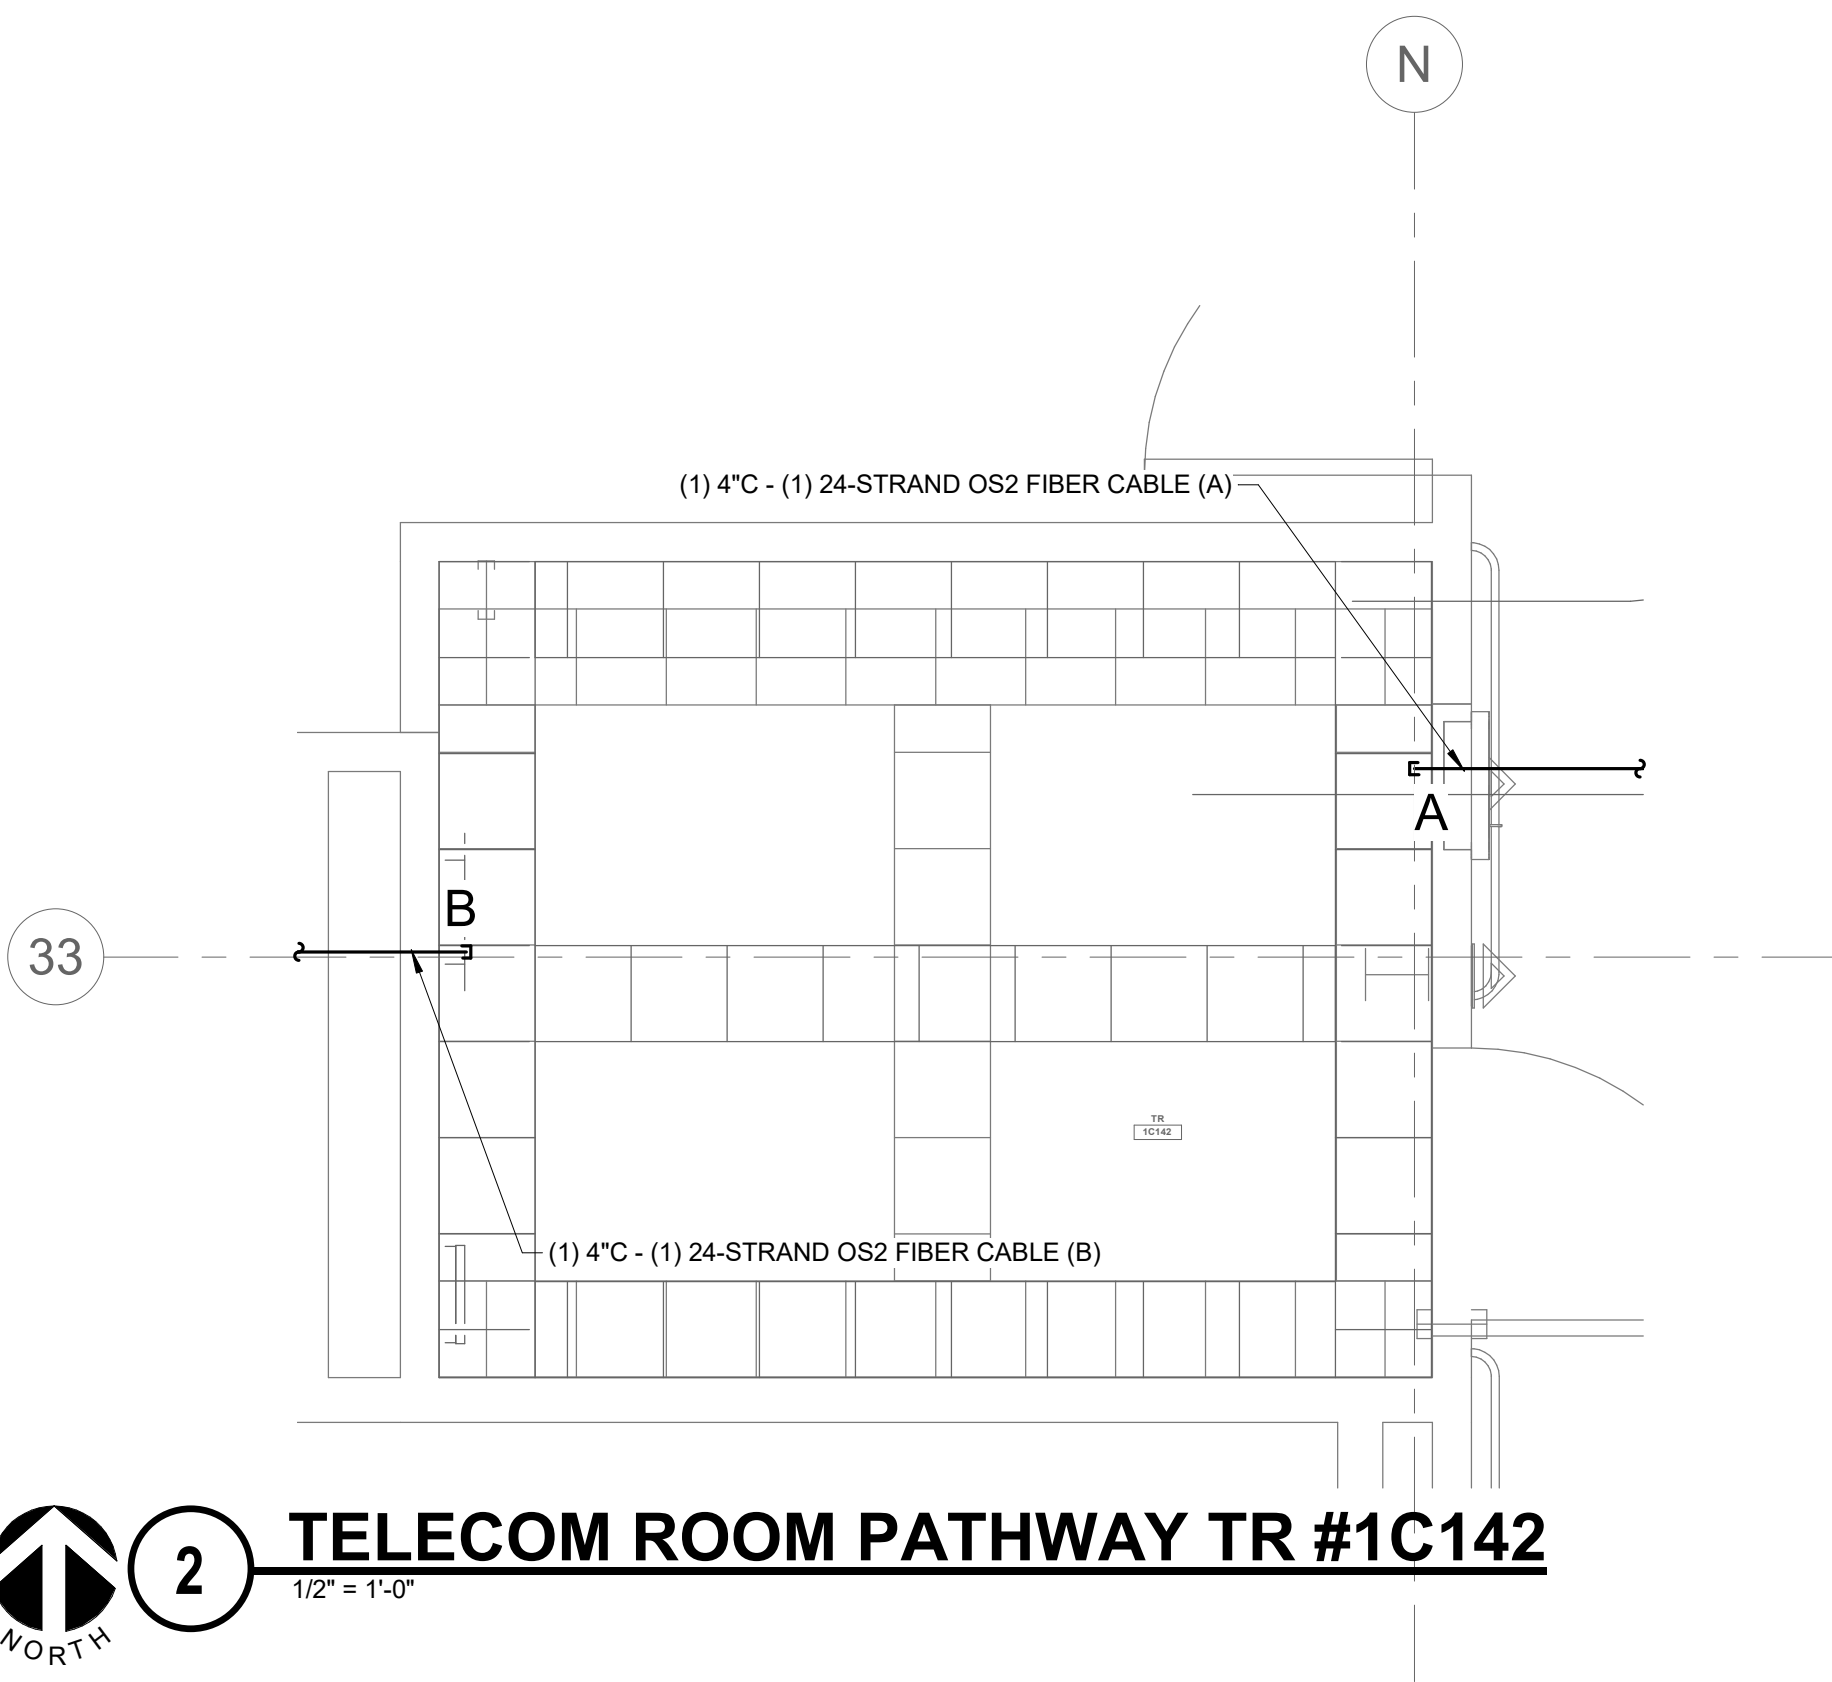


2 TELECOM ROOM PATHWAY TR #1C142
1/2" = 1'-0"

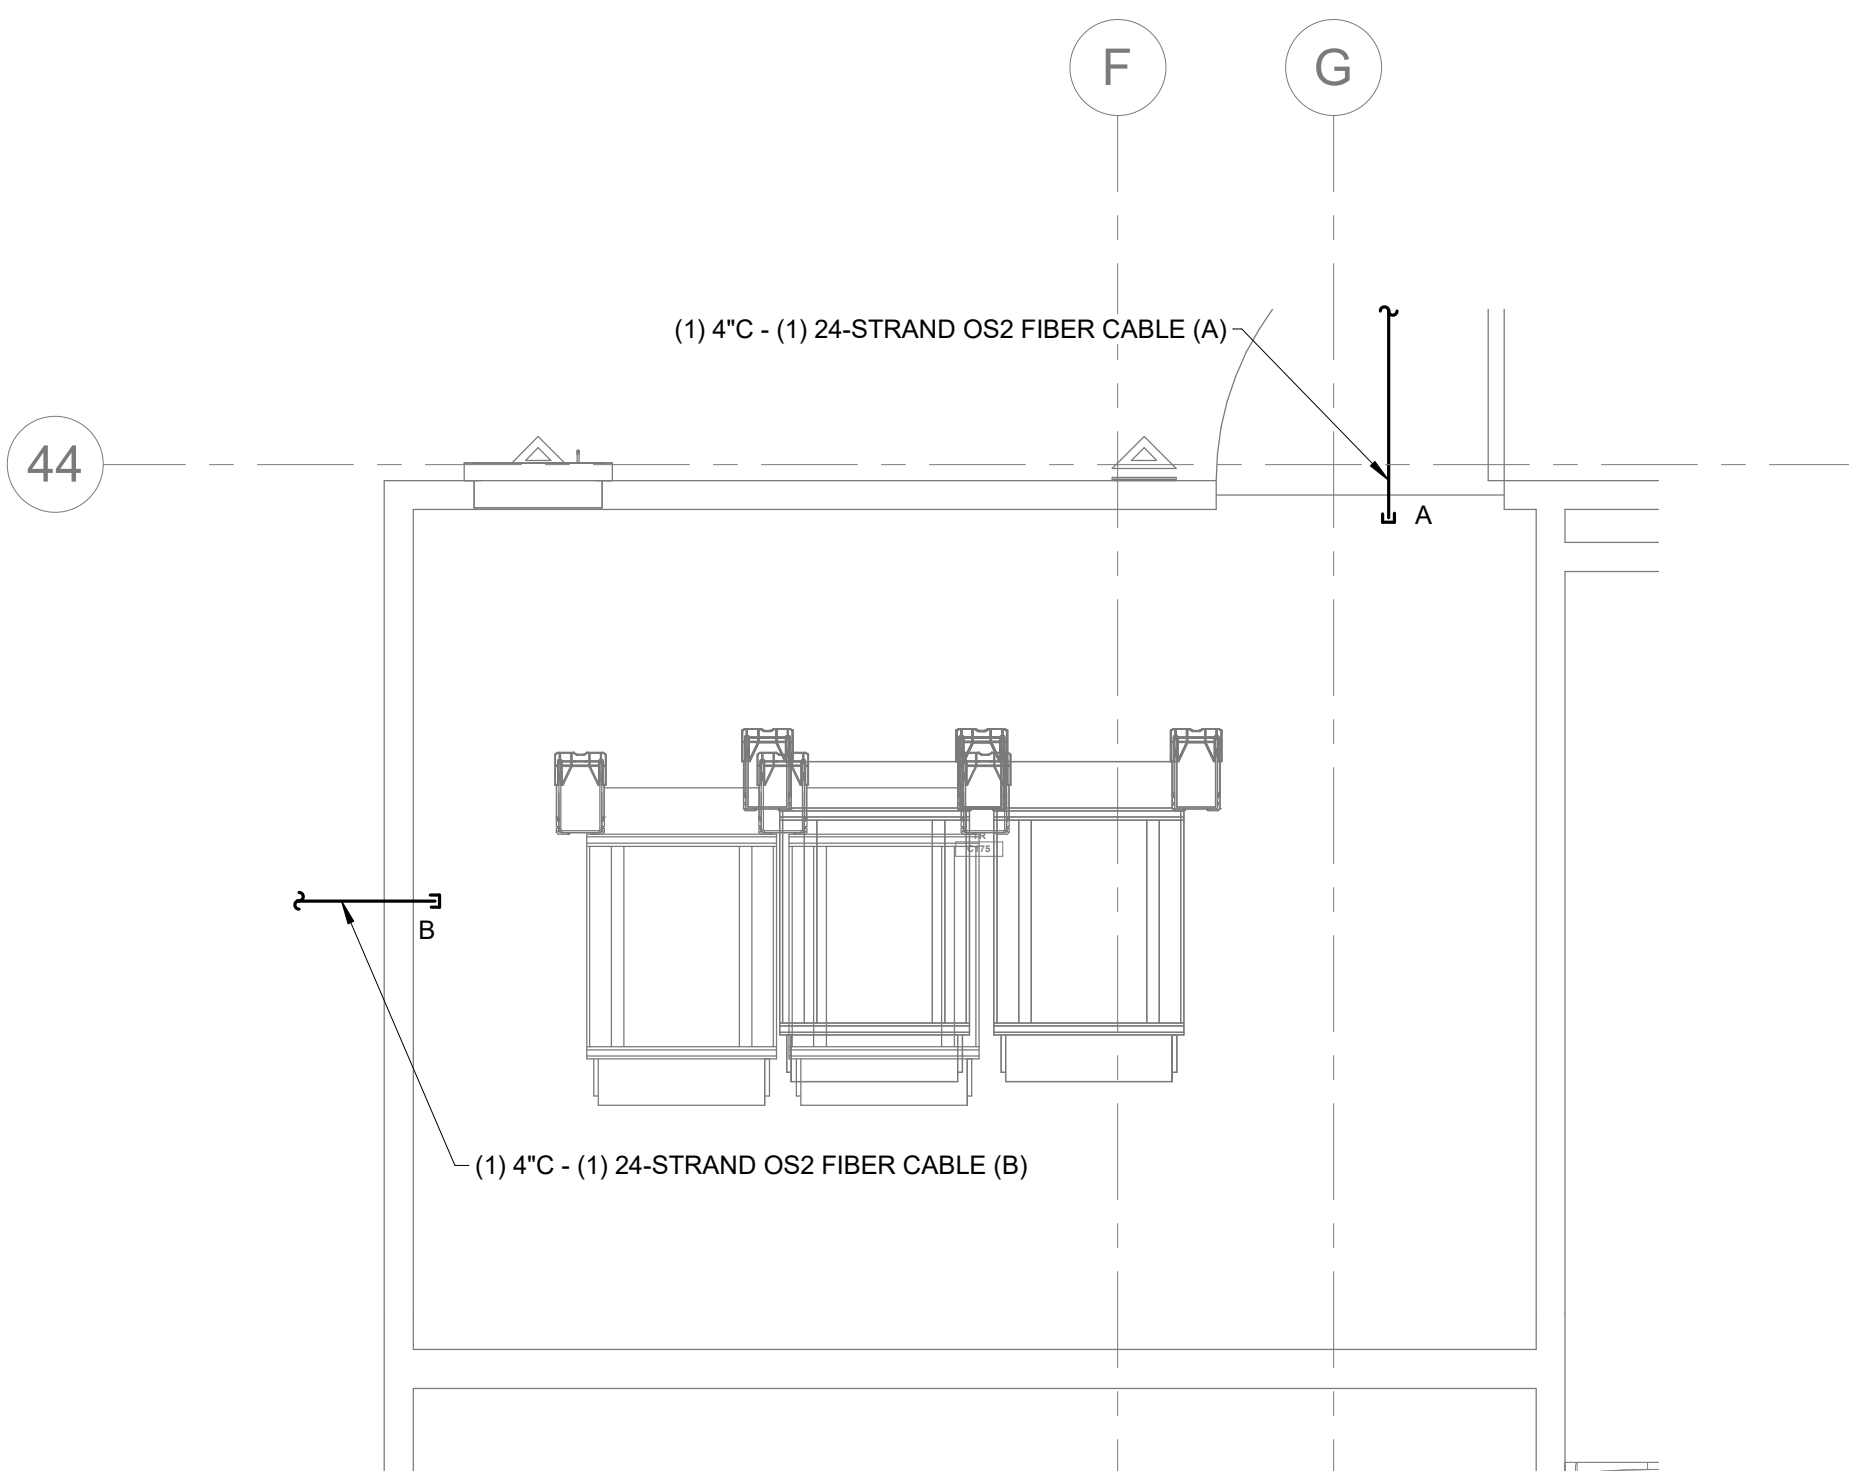

4 TELECOM ROOM ENLARGEMENT PLAN TR #C175
1/2" = 1'-0"
NOTES:
1. REFER TO ELECTRICAL DRAWINGS FOR ROOM LAYOUT AND RACK ELEVATIONS.
2. ROUTE OPTICAL FIBER CABLE TO OVERHEAD CABLE TRAY AND TERMINATE IN FIBER DISTRIBUTION CABINET.
KEYNOTES: **C** #
1. THROUGH WALL PENETRATION FOR BACKBONE CONDUIT. OPTICAL FIBER CABLE CONTINUES ON CABLE TRAY TO RACKS.

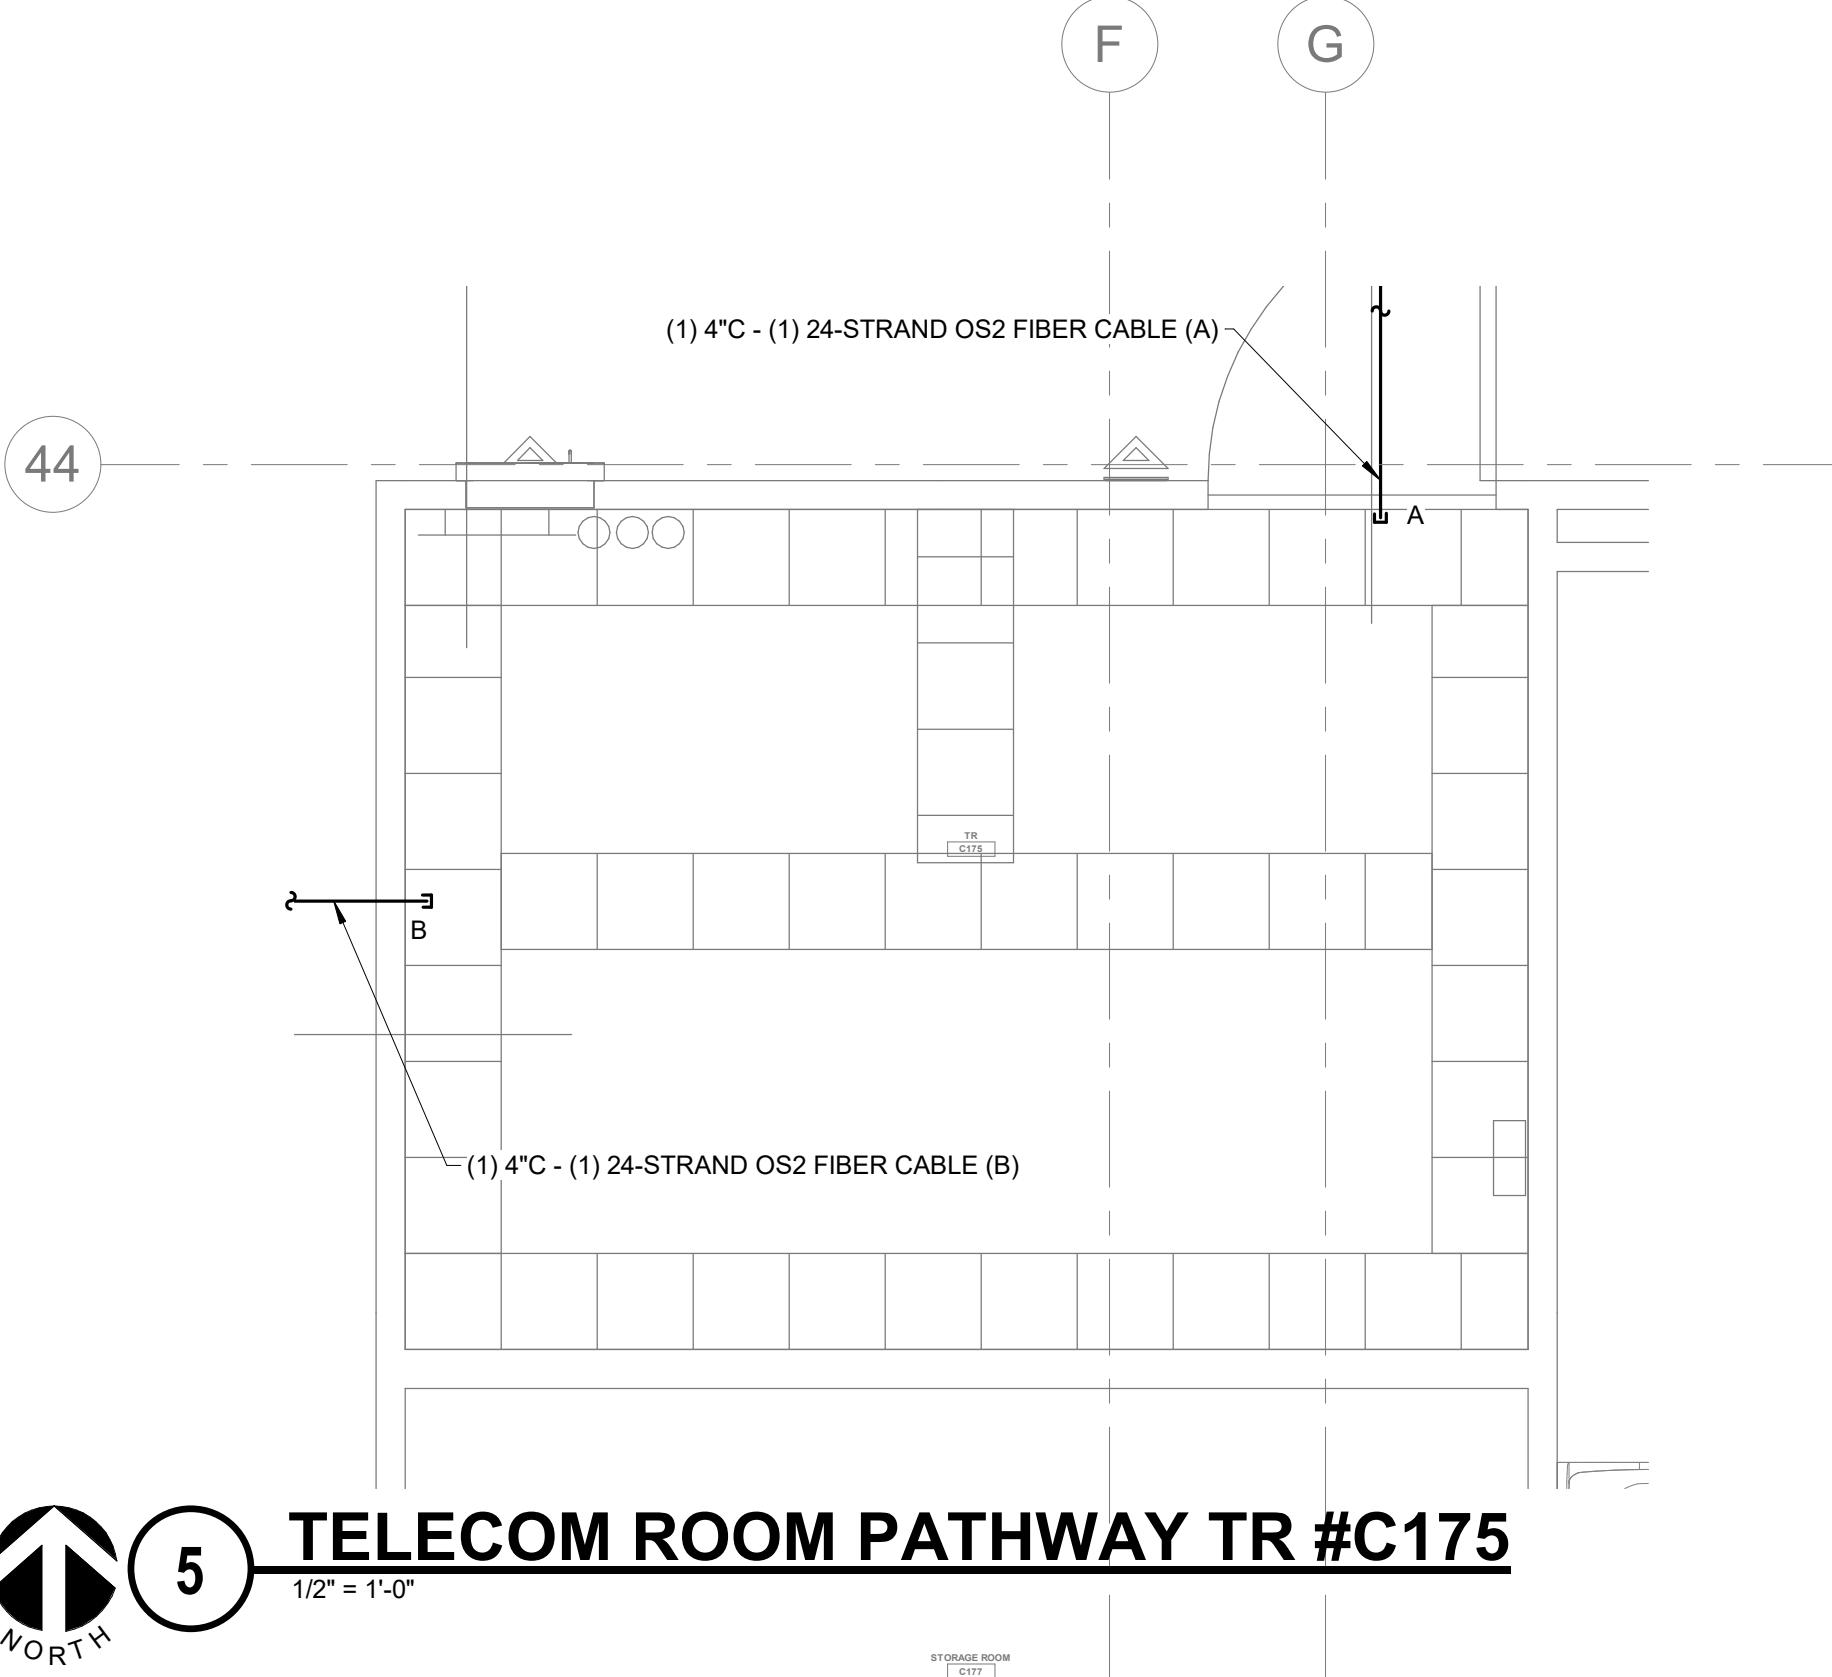

5 TELECOM ROOM PATHWAY TR #C175
1/2" = 1'-0"

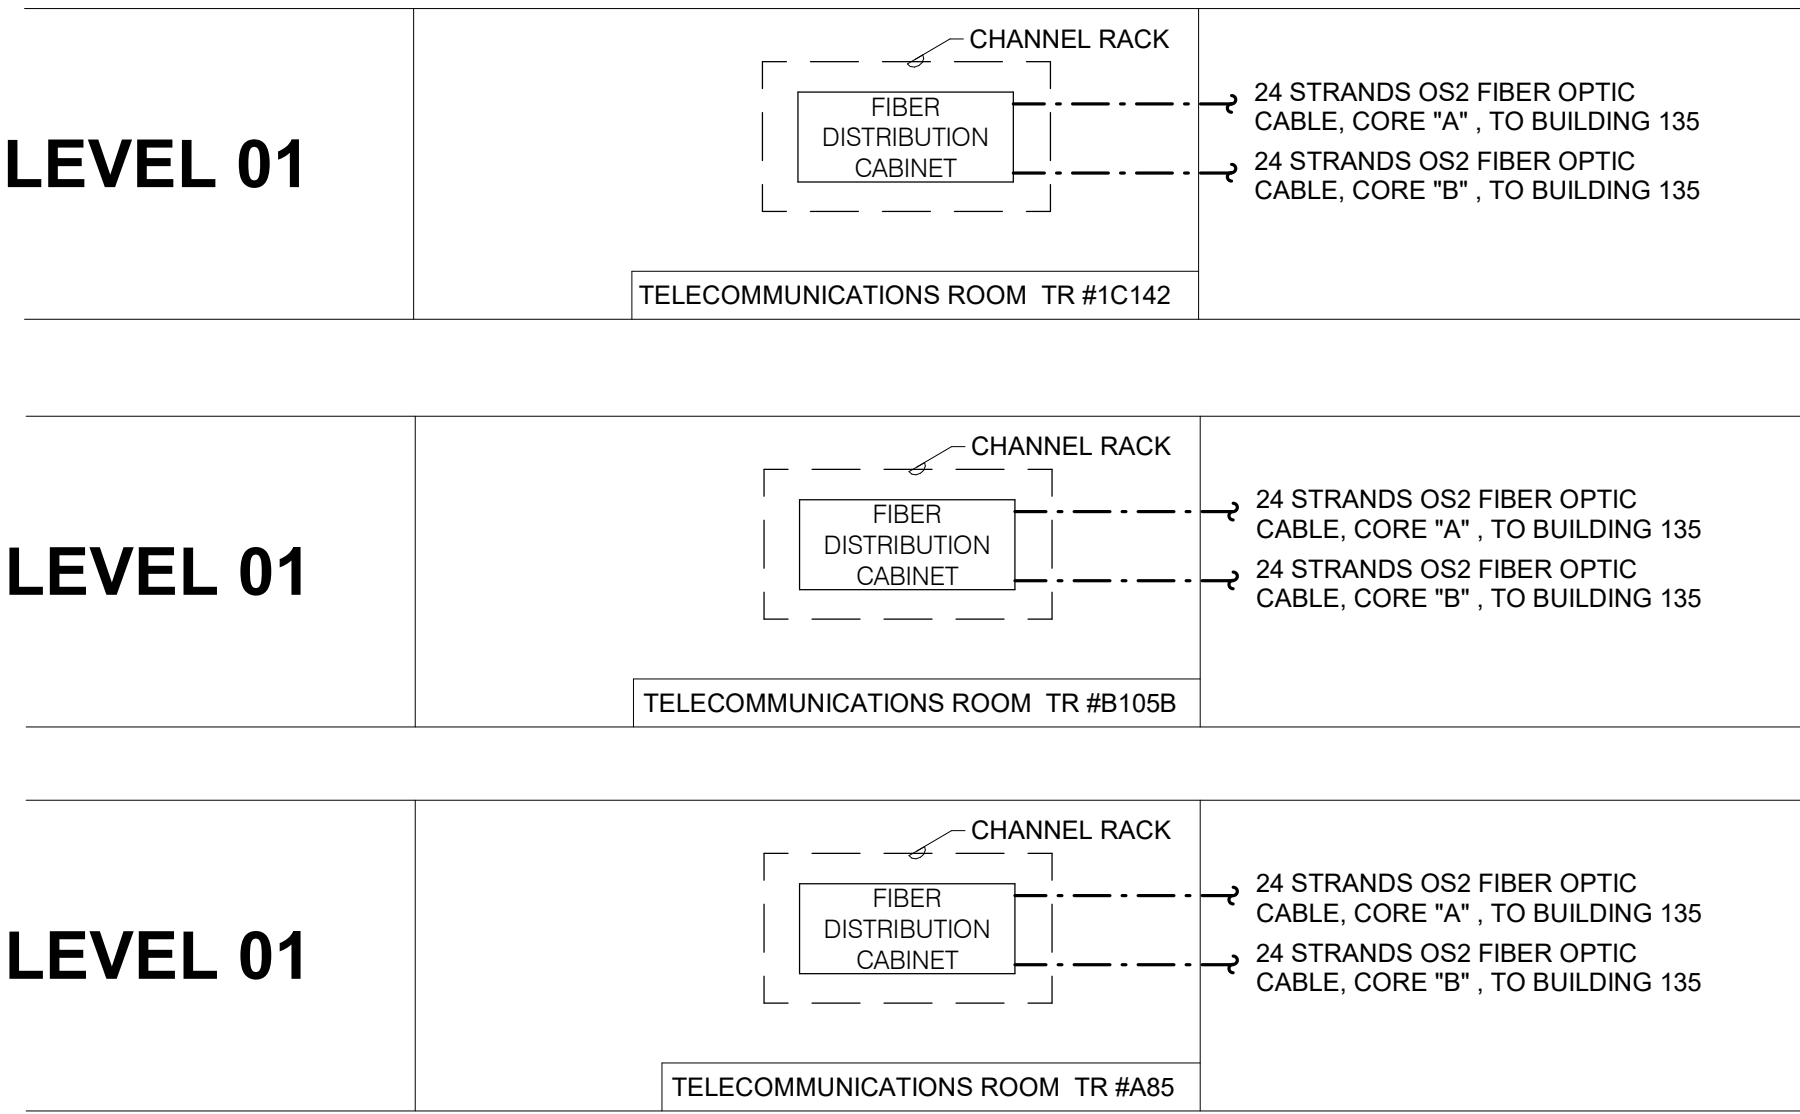

3 FIBER RISER DIAGRAM
NO SCALE
NOTES:
1. THIS RISER IS DIAGMATIC AND MAY NOT SHOW ACTUAL ROUTING OR QUANTITIES OF MATERIALS SHOWN. THIS RISER IS SHOWN FOR CLARIFICATION OF CONNECTIONS, LOCATIONS AND CABLE TYPE. ALL INFORMATION OUTLETS ARE TYPICAL OF THE OUTLETS IN THE AREA SHOWN. REFER TO FLOOR PLANS FOR MORE SPECIFIC ROUTING INFORMATION. REFER TO REQUIREMENTS.
2. REFER TO ELECTRICAL DRAWINGS FOR CHANNEL RACK AND FIBER OPTIC DISTRIBUTION CABINET SPECIFICATIONS

Revisions:	Date:

CONSULTANT
ENGINEERING DISCIPLINE:
IMEG
225 W WASHINGTON STREET SUITE 2700 CHICAGO, IL 60609 P: 312.294.0501 F: 312.294.0003 PROJECT #22010109.00

ARCHITECT/ENGINEER OF RECORD
A/E:
SPEES DESIGN BUILD 23830 PACIFIC HIGHWAY S. SUITE 203 KENT, WA 98032
SDB SPEESDESIGNBUILD

STAMP
Bicsi BICS COMMUNICATIONS DISTRIBUTION EMPLOYED 01/01/2025 RCDD

Office of Construction and Facilities Management
VA U.S. Department of Veterans Affairs

Drawing Title
BLDG.137 TECHNOLOGY ENLARGED PLANS
Approved:


Phase
100% CONSTRUCTION DOCUMENTS
FULLY SPRINKLERED

Project Title
EHRM INFRASTRUCTURE UPGRADES - HAMPTON
Location
HAMPTON VA MEDICAL CENTER, HAMPTON, VIRGINIA
Issue Date
05/09/2025
Checked
EW
Drawn
IMEG

Project Number
509-22-700
Building Number
137
Drawing Number
137T-401
695 of 713

- SHEET NOTES:**
1. REFER TO SITEPLAN TS001 FOR ADDITIONAL INFORMATION.
 2. REFER TO TS00 AND TS01 FOR CAMPUS OPTICAL FIBER CABLE RISER DIAGRAMS.
 3. REFER TO 217400 FOR HANDHOLE DETAIL.
 4. NEW BACKBONE OPTICAL FIBER CABLES SHALL BE INDOOR/OUTDOOR TYPE.
 5. ALL BACKBONE OPTICAL FIBER CABLE PATHWAYS SHALL BE NEW. DO NOT RE-USE EXISTING BACKBONE CABLE PATHWAYS FOR NEW BACKBONE CABLES.
 6. TRANSITION PVC CONDUITS TO GRC IN CRAWL SPACE OR EXPOSED EXTERIOR LOCATIONS. TRANSITION TO EMT CONDUITS AT INTERIOR OF BUILDING. SEAL ALL PENETRATIONS TO MAINTAIN FIRE-RATINGS OF WALL, CEILING AND FLOORS.

- KEYNOTES:** (1) (2)
1. PROVIDE PULLBOX ON EXTERIOR WALL AT HEIGHT OF FIRST FLOOR CEILING. ROUTE CONDUIT FROM HANDHOLE UP WALL INTO PULLBOX. PROVIDE PENETRATIONS THRU WALLS AND CONTINUE ROUTE ABOVE. CORRIDOR FINISHED CEILING OVER INTO TR #149.
 2. ROUTE CONDUITS INTO TR #149 AT ABOVE HEIGHT OF CABLE TRAY. PROVIDE PULLBOX AND ROUTE CONDUIT TO LOCATION BELOW TR #251. PROVIDE PENETRATIONS THRU CEILING DECK AND ROUTE CONDUITS UP INTO TR #251.

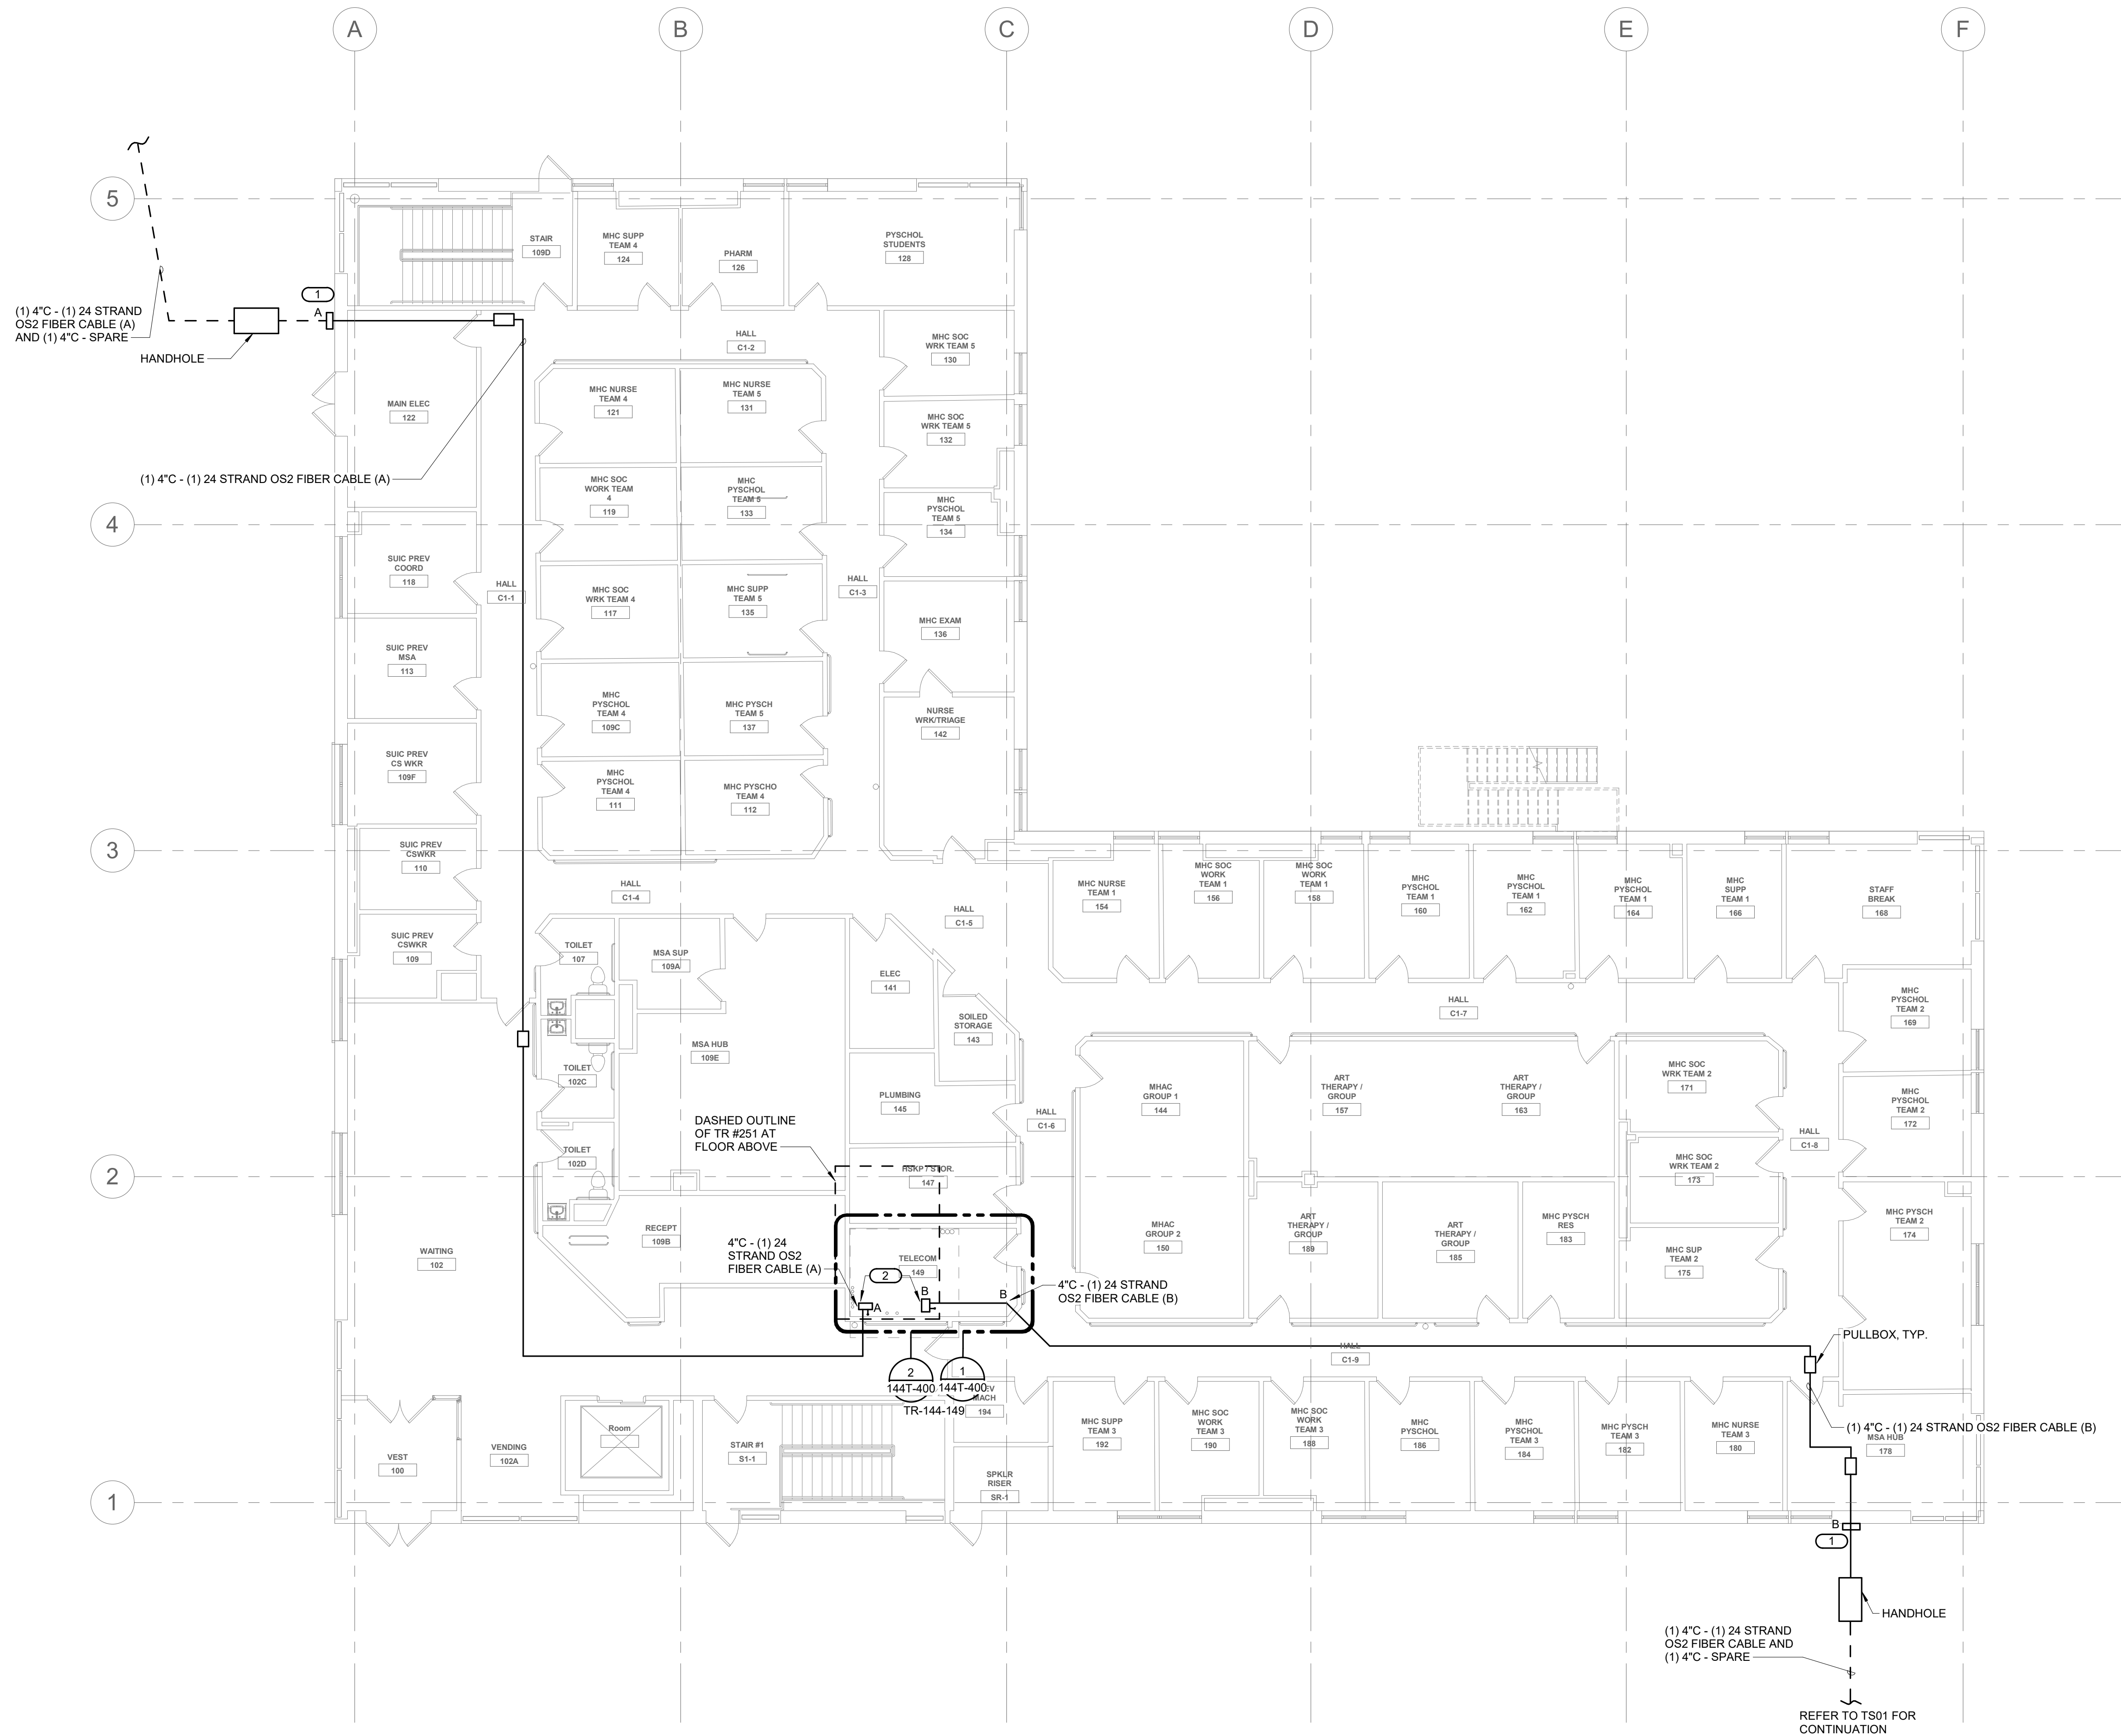

1 LEVEL 01 PLAN - TECHNOLOGY
1/8\"/>


--	--	

SHEET NOTES:

1. REFER TO SITEPLAN TS001 FOR ADDITIONAL INFORMATION.
2. REFER TO TS500 AND TS01 FOR CAMPUS OPTICAL FIBER CABLE RISER DIAGRAMS.
3. REFER TO 2T4700 FOR HANDHOLE DETAIL.
4. NEW BACKBONE OPTICAL FIBER CABLES SHALL BE INDOOR/OUTDOOR TYPE.
5. ALL BACKBONE OPTICAL FIBER CABLE PATHWAYS SHALL BE NEW AND NOT REUSE EXISTING BACKBONE CABLE PATHWAYS FOR NEW BACKBONE CABLES.
6. TRANSITION PVC CONDUITS TO GRC IN CRAWL SPACE OR EXPOSED EXTERIOR LOCATIONS. TRANSITION TO EMT CONDUITS AT INTERIOR OF BUILDING.


KEY NOTES: #

1. ROUTE CONDUIT UP THRU FLOOR FROM TR #149 AT FLOOR BELOW. CONTINUE ROUTE OF CONDUIT UP TO ABOVE CABLE TRAY.

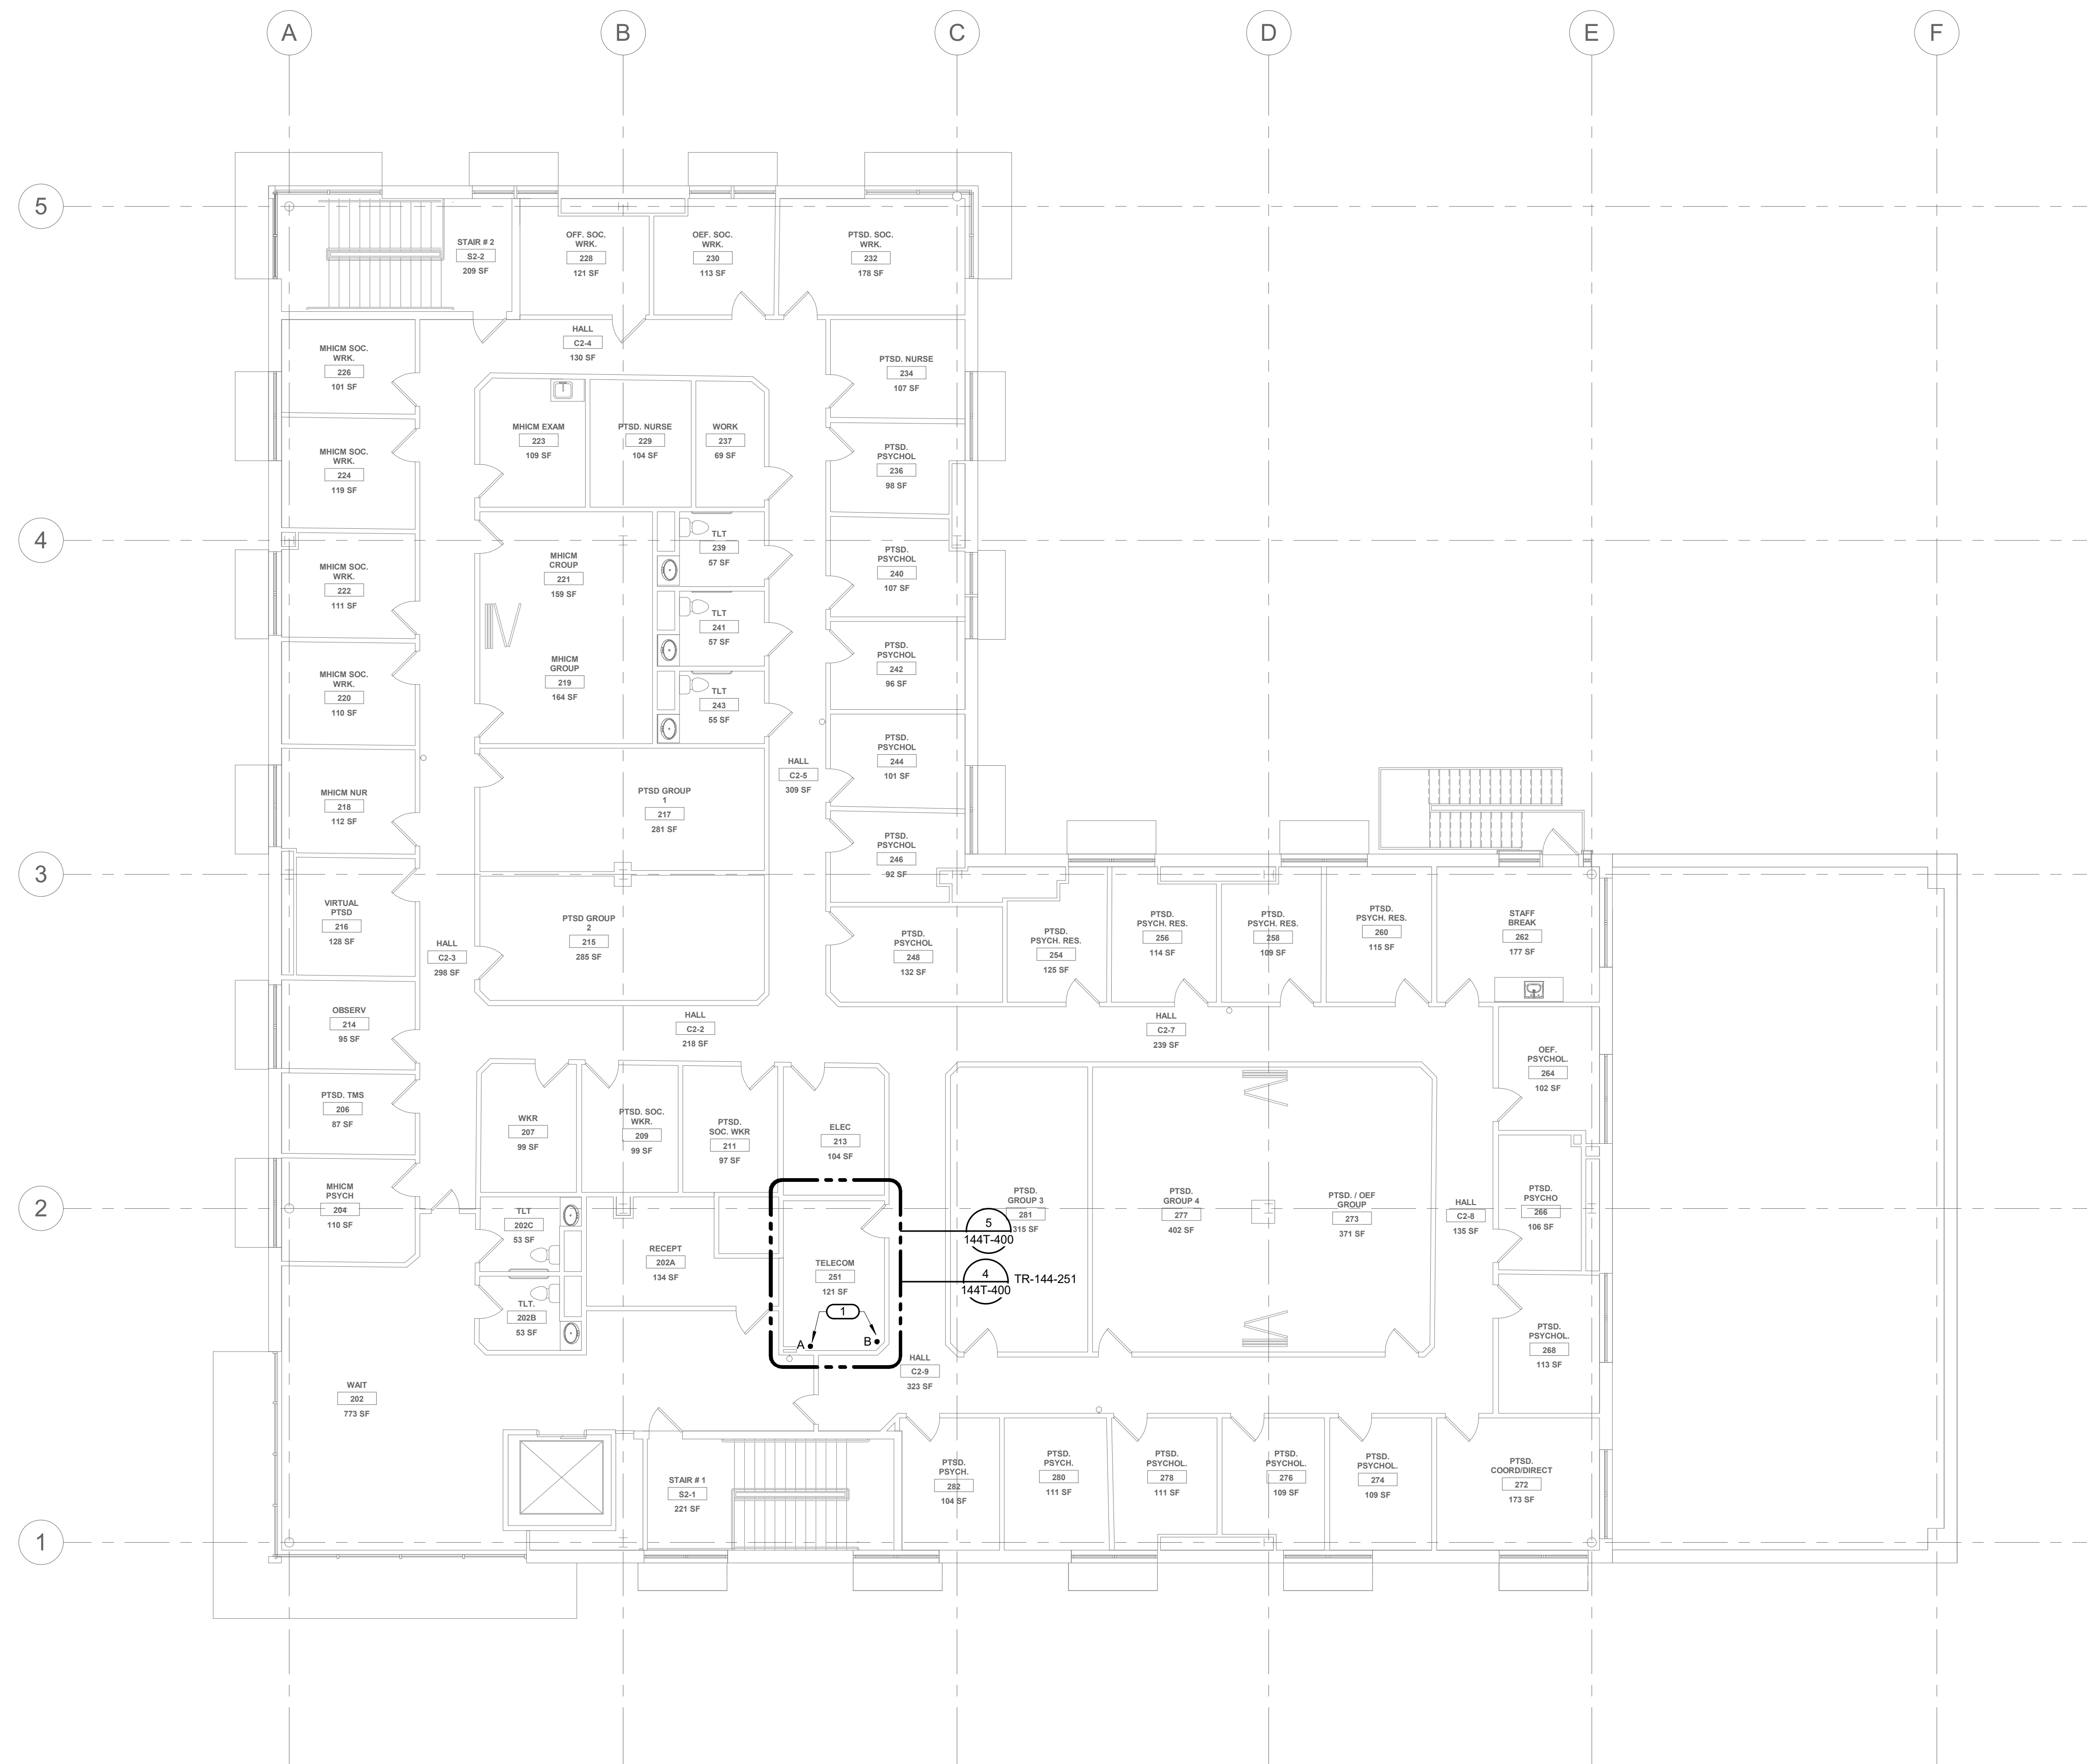

1 LEVEL 02 PLAN - TECHNOLOGY

1/8" = 1'-0"

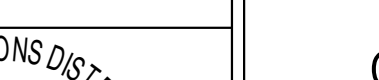		CONSULTANT ENGINEERING DISCIPLINE:  www.imegcorp.com 225 W WASHINGTON STREET SUITE 2700 CHICAGO, IL 60606 P: 312.294.0501 F: 312.294.0003 PROJECT #22010109.00	ARCHITECT/ENGINEER OF RECORD A/E: SPEES DESIGN BUILD 23830 PACIFIC HIGHWAY S. SUITE 203 KENT, WA 98032  SPEESDESIGNBUILD	STAMP 	Office of Construction and Facilities Management VA U.S. Department of Veterans Affairs	Drawing Title LEVEL 02 PLAN - TECHNOLOGY Approved:	Phase 100% CONSTRUCTION DOCUMENTS FULLY SPRINKLERED	Project Title EHRM INFRASTRUCTURE UPGRADES - HAMPTON Location HAMPTON VA MEDICAL CENTER, HAMPTON, VIRGINIA Issue Date 05/09/2025 Checked EW Drawn IMEG	Project Number 509-22-700 Building Number 144 Drawing Number 144T-102 697 of 713
Revisions:		Date:							

BM 360/509-22-700
VA Hampton
EHRM 509-22-700 B144T_R01.rvt

8/21/2025 7:04:40 AM

VA FORM 08 - 6231


Revisions:	Date:

CONSULTANT
ENGINEERING DISCIPLINE:
IMEG
www.imegcorp.com
225 W WASHINGTON STREET
SUITE 2700
CHICAGO, IL 60606
P: 312.294.0501 F: 312.294.0003
PROJECT #22010109.00

ARCHITECT/ENGINEER OF RECORD
A/E:
SPEES DESIGN BUILD
23830 PACIFIC HIGHWAY S. SUITE 203
KENT, WA 98032



STAMP

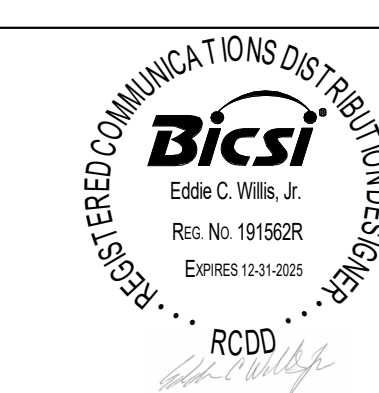

Office of
Construction
and Facilities
Management



U.S. Department
of Veterans Affairs

Drawing Title
TECHNOLOGY ENLARGED PLANS

Approved:

Phase
100% CONSTRUCTION
DOCUMENTS

FULLY SPRINKLERED

Project Title
EHRM INFRASTRUCTURE
UPGRADES - HAMPTON

Location
HAMPTON VA MEDICAL CENTER, HAMPTON, VIRGINIA

Issue Date
05/09/2025

Checked
EW

Drawn
IMEG

Project Number
509-22-700
Building Number
144

Drawing Number
144T-400

698 of 713



1

TELECOM ROOM ENLARGEMENT PLAN - TR-144-149

1/2" = 1'-0"

NOTES:

1. REFER TO ELECTRICAL DRAWINGS FOR ROOM LAYOUT AND RACK ELEVATIONS.
2. ROUTE OPTICAL FIBER CABLES TO OVERHEAD CABLE TRAYS AND TERMINATE IN FIBER DISTRIBUTION CABINET.



2

TELECOM ROOM PATHWAYS - TR-144-149

1/2" = 1'-0"

KEYNOTES:

1. THROUGH WALL PENETRATION FOR BACKBONE CONDUIT. OPTICAL FIBER CABLES CONTINUE ON CABLE TRAY TO RACKS.



4

TELECOM ROOM ENLARGEMENT PLAN - TR-144-251

1/2" = 1'-0"

NOTES:

1. REFER TO ELECTRICAL DRAWINGS FOR ROOM LAYOUT AND RACK ELEVATIONS.
2. ROUTE OPTICAL FIBER CABLES TO OVERHEAD CABLE TRAYS AND TERMINATE IN FIBER DISTRIBUTION CABINET.



7


TELECOM ROOM PATHWAYS - TR-144-251

1/2" = 1'-0"


KEYNOTES:

1. THROUGH FLOOR/CEILING PENETRATION FOR BACKBONE CONDUIT. CONTINUE CONDUIT UP TO ABOVE CABLE TRAY. OPTICAL FIBER CABLES CONTINUE ON CABLE TRAY TO RACKS.

LEVEL 02

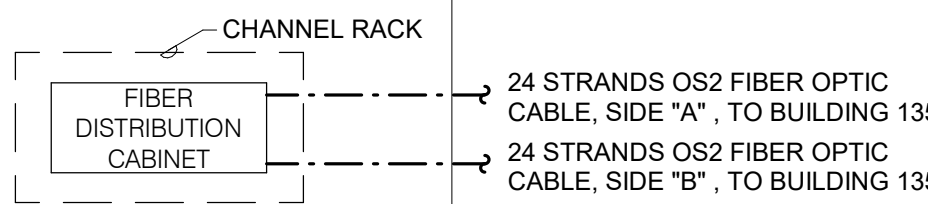

LEVEL 01

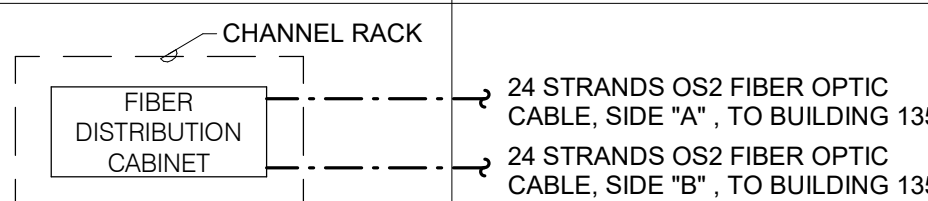


3

FIBER RISER DIAGRAM


NO SCALE

NOTES:

1. THIS RISER IS DIAGRAMMATIC AND MAY NOT SHOW ACTUAL ROUTING OR QUANTITIES OF MATERIALS SHOWN. THIS RISER IS SHOWN FOR CLARIFICATION OF CONNECTION(S), LOCATIONS AND CABLE TYPE. ALL INFORMATION OUTLETS ARE TYPICAL OF THE OUTLETS IN THE AREA SHOWN. REFER TO FLOOR PLANS FOR MORE SPECIFIC ROUTING INFORMATION. REFER TO SPECIFICATIONS FOR ADDITIONAL REQUIREMENTS.
2. REFER TO ELECTRICAL DRAWINGS FOR CHANNEL RACK AND FIBER OPTIC DISTRIBUTION CABINET SPECIFICATIONS

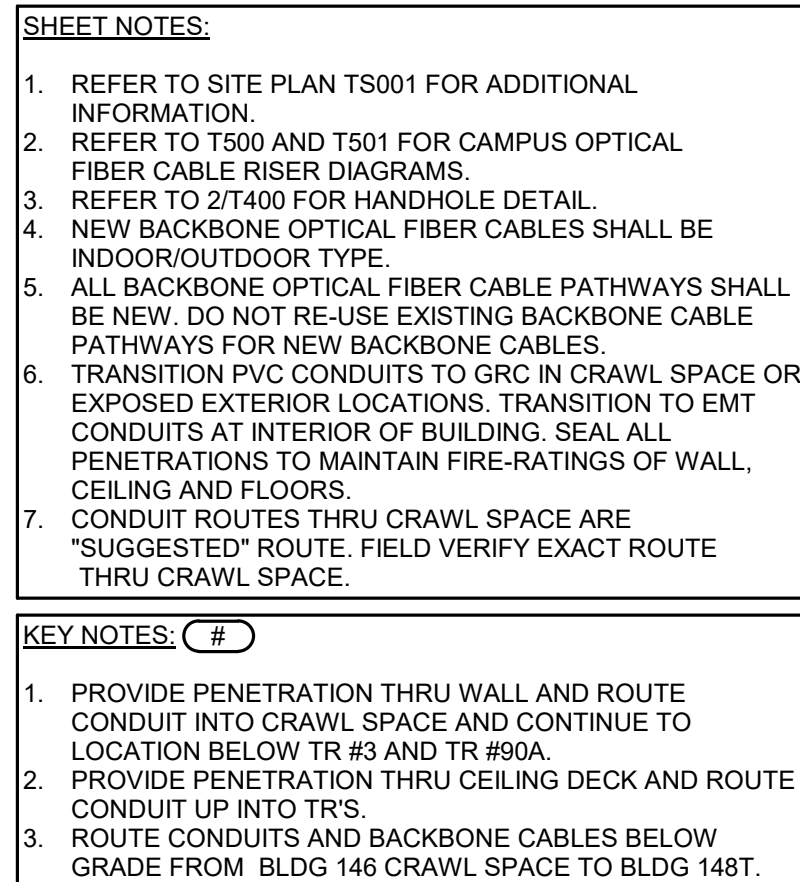

BIM 360://509-22-700
VAHampton
EHRM/509-700.B146.T_R21.rvt

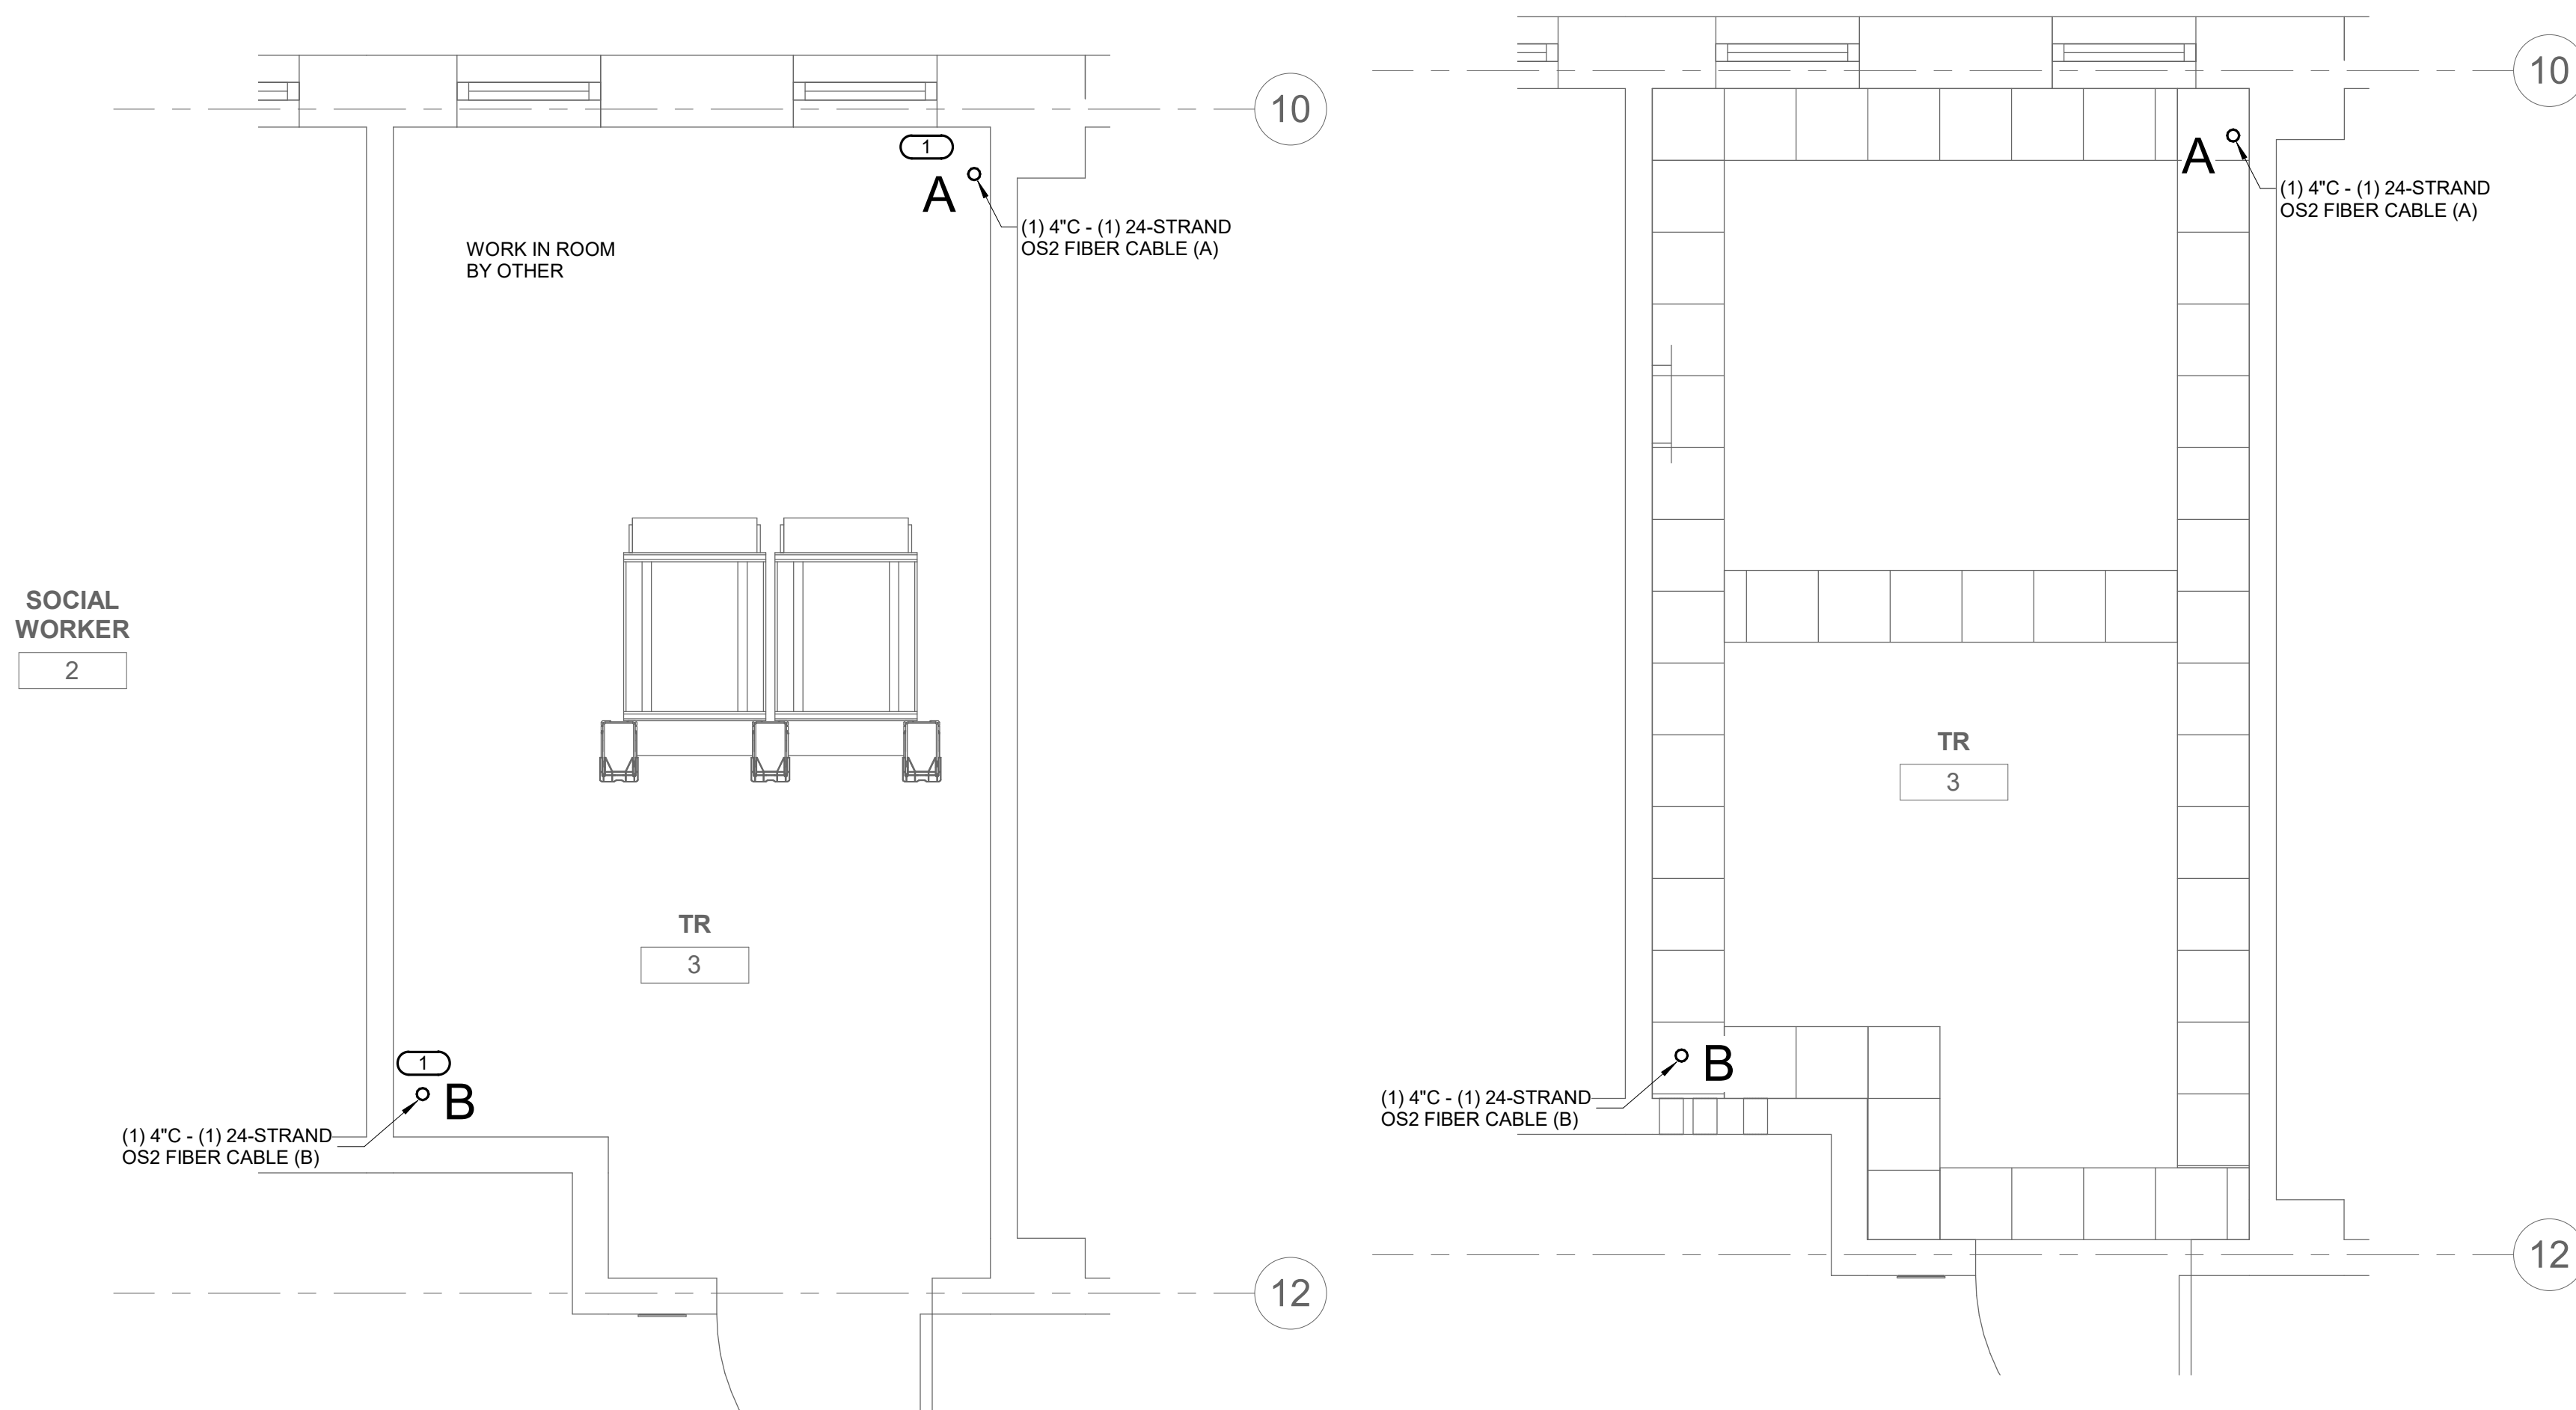

 TELECOM ROOM ENLARGEMENT TR #3

1/2" = 1'-0"


 2 TELECOM ROOM PATHWAY TR #3

$$1/2'' = 1'-0''$$

1. REFER TO ELECTRICAL DRAWINGS FOR ROOM LAYOUT AND RACK ELEVATIONS.
2. ROUTE OPTICAL FIBER CABLE TO OVERHEAD CABLE TRAY AND TERMINATE IN FIBER DISTRIBUTION CABINET.

KEYNOTES:

1. THROUGH FLOOR PENETRATION FOR BACKBONE CONDUIT. OPTICAL FIBER CABLE CONTINUES ON CABLE TRAY TO RACKS.

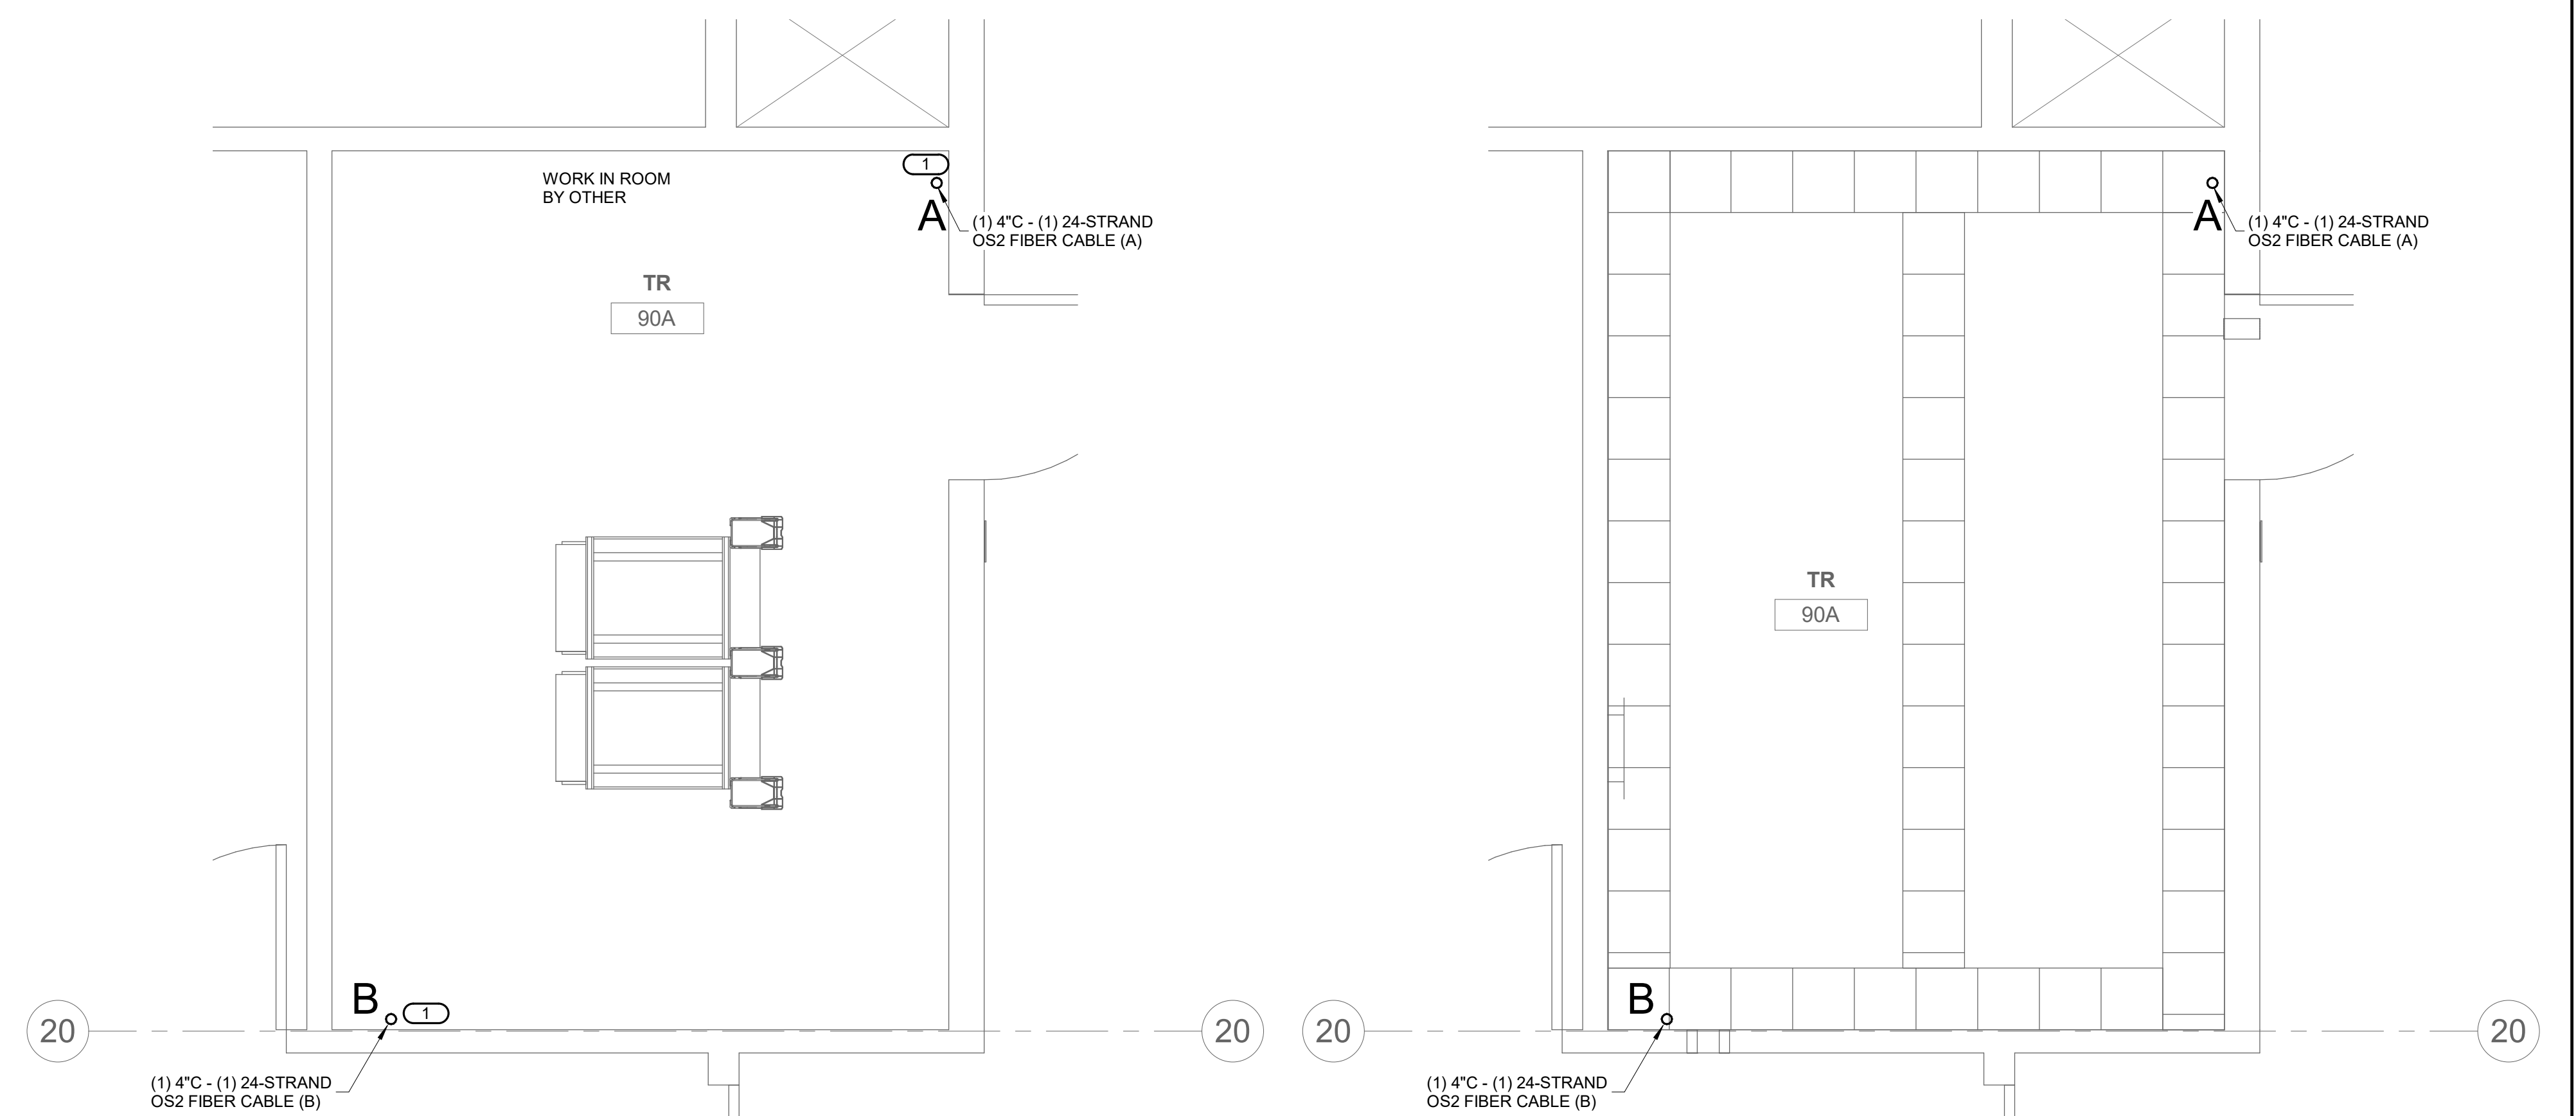

 3 TELECOM ROOM ENLARGEMENT TR #90A

$$1/2'' = 1'-0''$$


1. REFER TO ELECTRICAL DRAWINGS FOR ROOM LAYOUT AND RACK ELEVATIONS.
2. ROUTE OPTICAL FIBER CABLE TO OVERHEAD CABLE TRAY AND TERMINATE IN FIBER DISTRIBUTION CABINET.

 4 TELECOM ROOM PATHWAY TR #90A
1/2" = 1'-0"

 $1/2 = 1/4$

- KEYNOTES: #


1. THROUGH FLOOR PENETRATION FOR BACKBONE CONDUIT. OPTICAL FIBER CABLE CONTINUES ON CABLE TRAY TO RACKS.

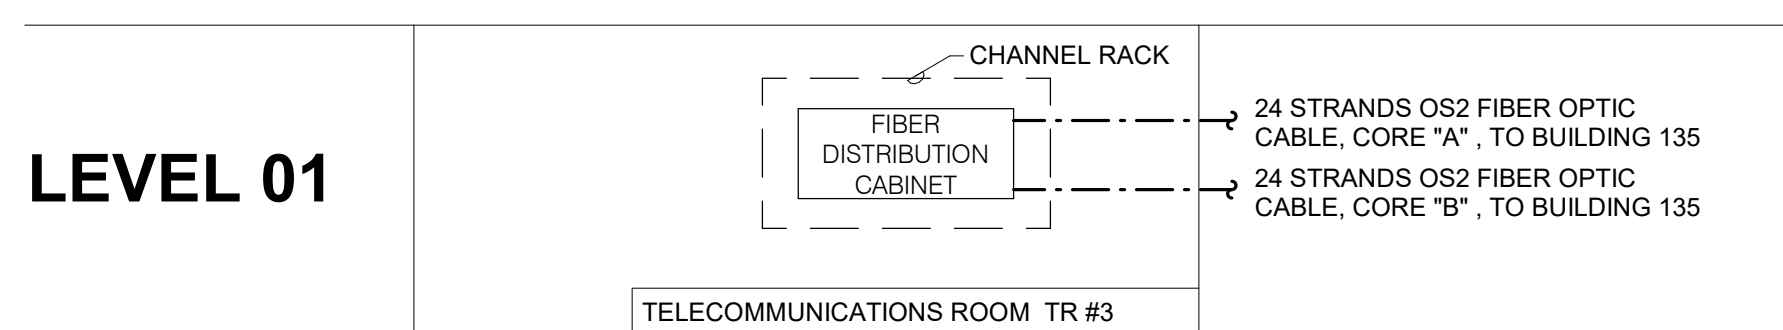

5 FIBER RISER DIAGRAM
NO SCALE

NO SCALE

- NOTES:**
1. THIS RISER IS DIAGRAMMATIC AND MAY NOT SHOW ACTUAL ROUTING OR QUANTITIES OF MATERIALS SHOWN. THIS RISER IS SHOWN FOR CLARIFICATION OF CONNECTION(S), LOCATIONS AND CABLE TYPE. ALL INFORMATION OUTLETS ARE TYPICAL OF THE OUTLETS IN THE AREA SHOWN. REFER TO FLOOR PLANS FOR MORE SPECIFIC ROUTING INFORMATION. REFER TO SPECIFICATIONS FOR ADDITIONAL REQUIREMENTS.
 2. REFER TO ELECTRICAL DRAWINGS FOR CHANNEL RACK AND FIBER OPTIC DISTRIBUTION CABINET SPECIFICATIONS

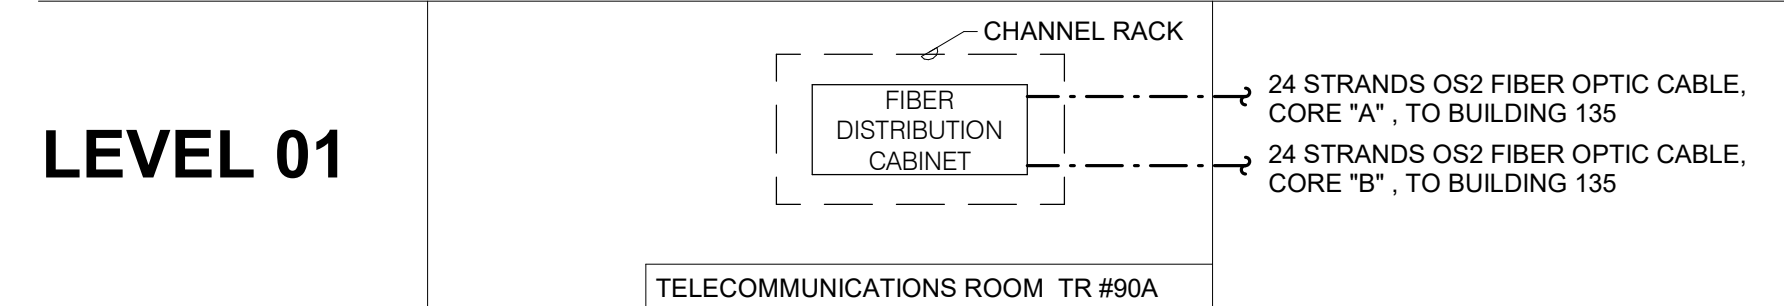

6 FIBER RISER DIAGRAM
NO SCALE


NO SCALE

- NOTES:**
1. THIS RISER IS DIAGRAMMATIC AND MAY NOT SHOW ACTUAL ROUTING OR QUANTITIES OF MATERIALS SHOWN. THIS RISER IS SHOWN FOR CLARIFICATION OF CONNECTION(S), LOCATIONS AND CABLE TYPE. ALL INFORMATION OUTLETS ARE TYPICAL OF THE OUTLETS IN THE AREA SHOWN. REFER TO FLOOR PLANS FOR MORE SPECIFIC ROUTING INFORMATION. REFER TO SPECIFICATIONS FOR ADDITIONAL REQUIREMENTS.
 2. REFER TO ELECTRICAL DRAWINGS FOR CHANNEL RACK AND FIBER OPTIC DISTRIBUTION CABINET SPECIFICATIONS

[illegible]

A
B
C
D
E
F

- SHEET NOTES:**
 - REFER TO SITEPLAN TS001 FOR ADDITIONAL INFORMATION.
 - REFER TO TS00 AND TS01 FOR CAMPUS OPTICAL FIBER CABLE RISER DIAGRAMS.
 - REFER TO 27400 FOR HANDHOLE DETAIL.
 - NEW BACKBONE OPTICAL FIBER CABLES SHALL BE INDOOR/OUTDOOR TYPE.
 - ALL BACKBONE OPTICAL FIBER CABLE PATHWAYS SHALL BE NEW. DO NOT RE-USE EXISTING BACKBONE CABLE PATHWAYS FOR NEW BACKBONE CABLES.
 - TRANSITION PVC CONDUITS TO GRC IN CRAWL SPACE OR EXPOSED EXTERIOR LOCATIONS. TRANSITION TO EMT CONDUITS AT INTERIOR OF BUILDING. SEAL ALL PENETRATIONS TO MAINTAIN FIRE-RATINGS OF WALL, CEILING AND FLOORS.
- KEY NOTES: (#)**
 - PROVIDE PULLBOX ON EXTERIOR WALL AT HEIGHT ABOVE CABLE TRAY IN TR #A8185 AND TR #D185. ROUTE CONDUIT UP WALL INTO PULLBOX. PROVIDE PENETRATION THRU WALL AND ROUTE CONDUIT THRU WALL INTO TRs ABOVE CABLE TRAY.
 - PROVIDE PULLBOX ABOVE CORRIDOR CEILING AND SEPARATE FIBER CABLES TO ROUTE TO OTHER TR INDICATED.

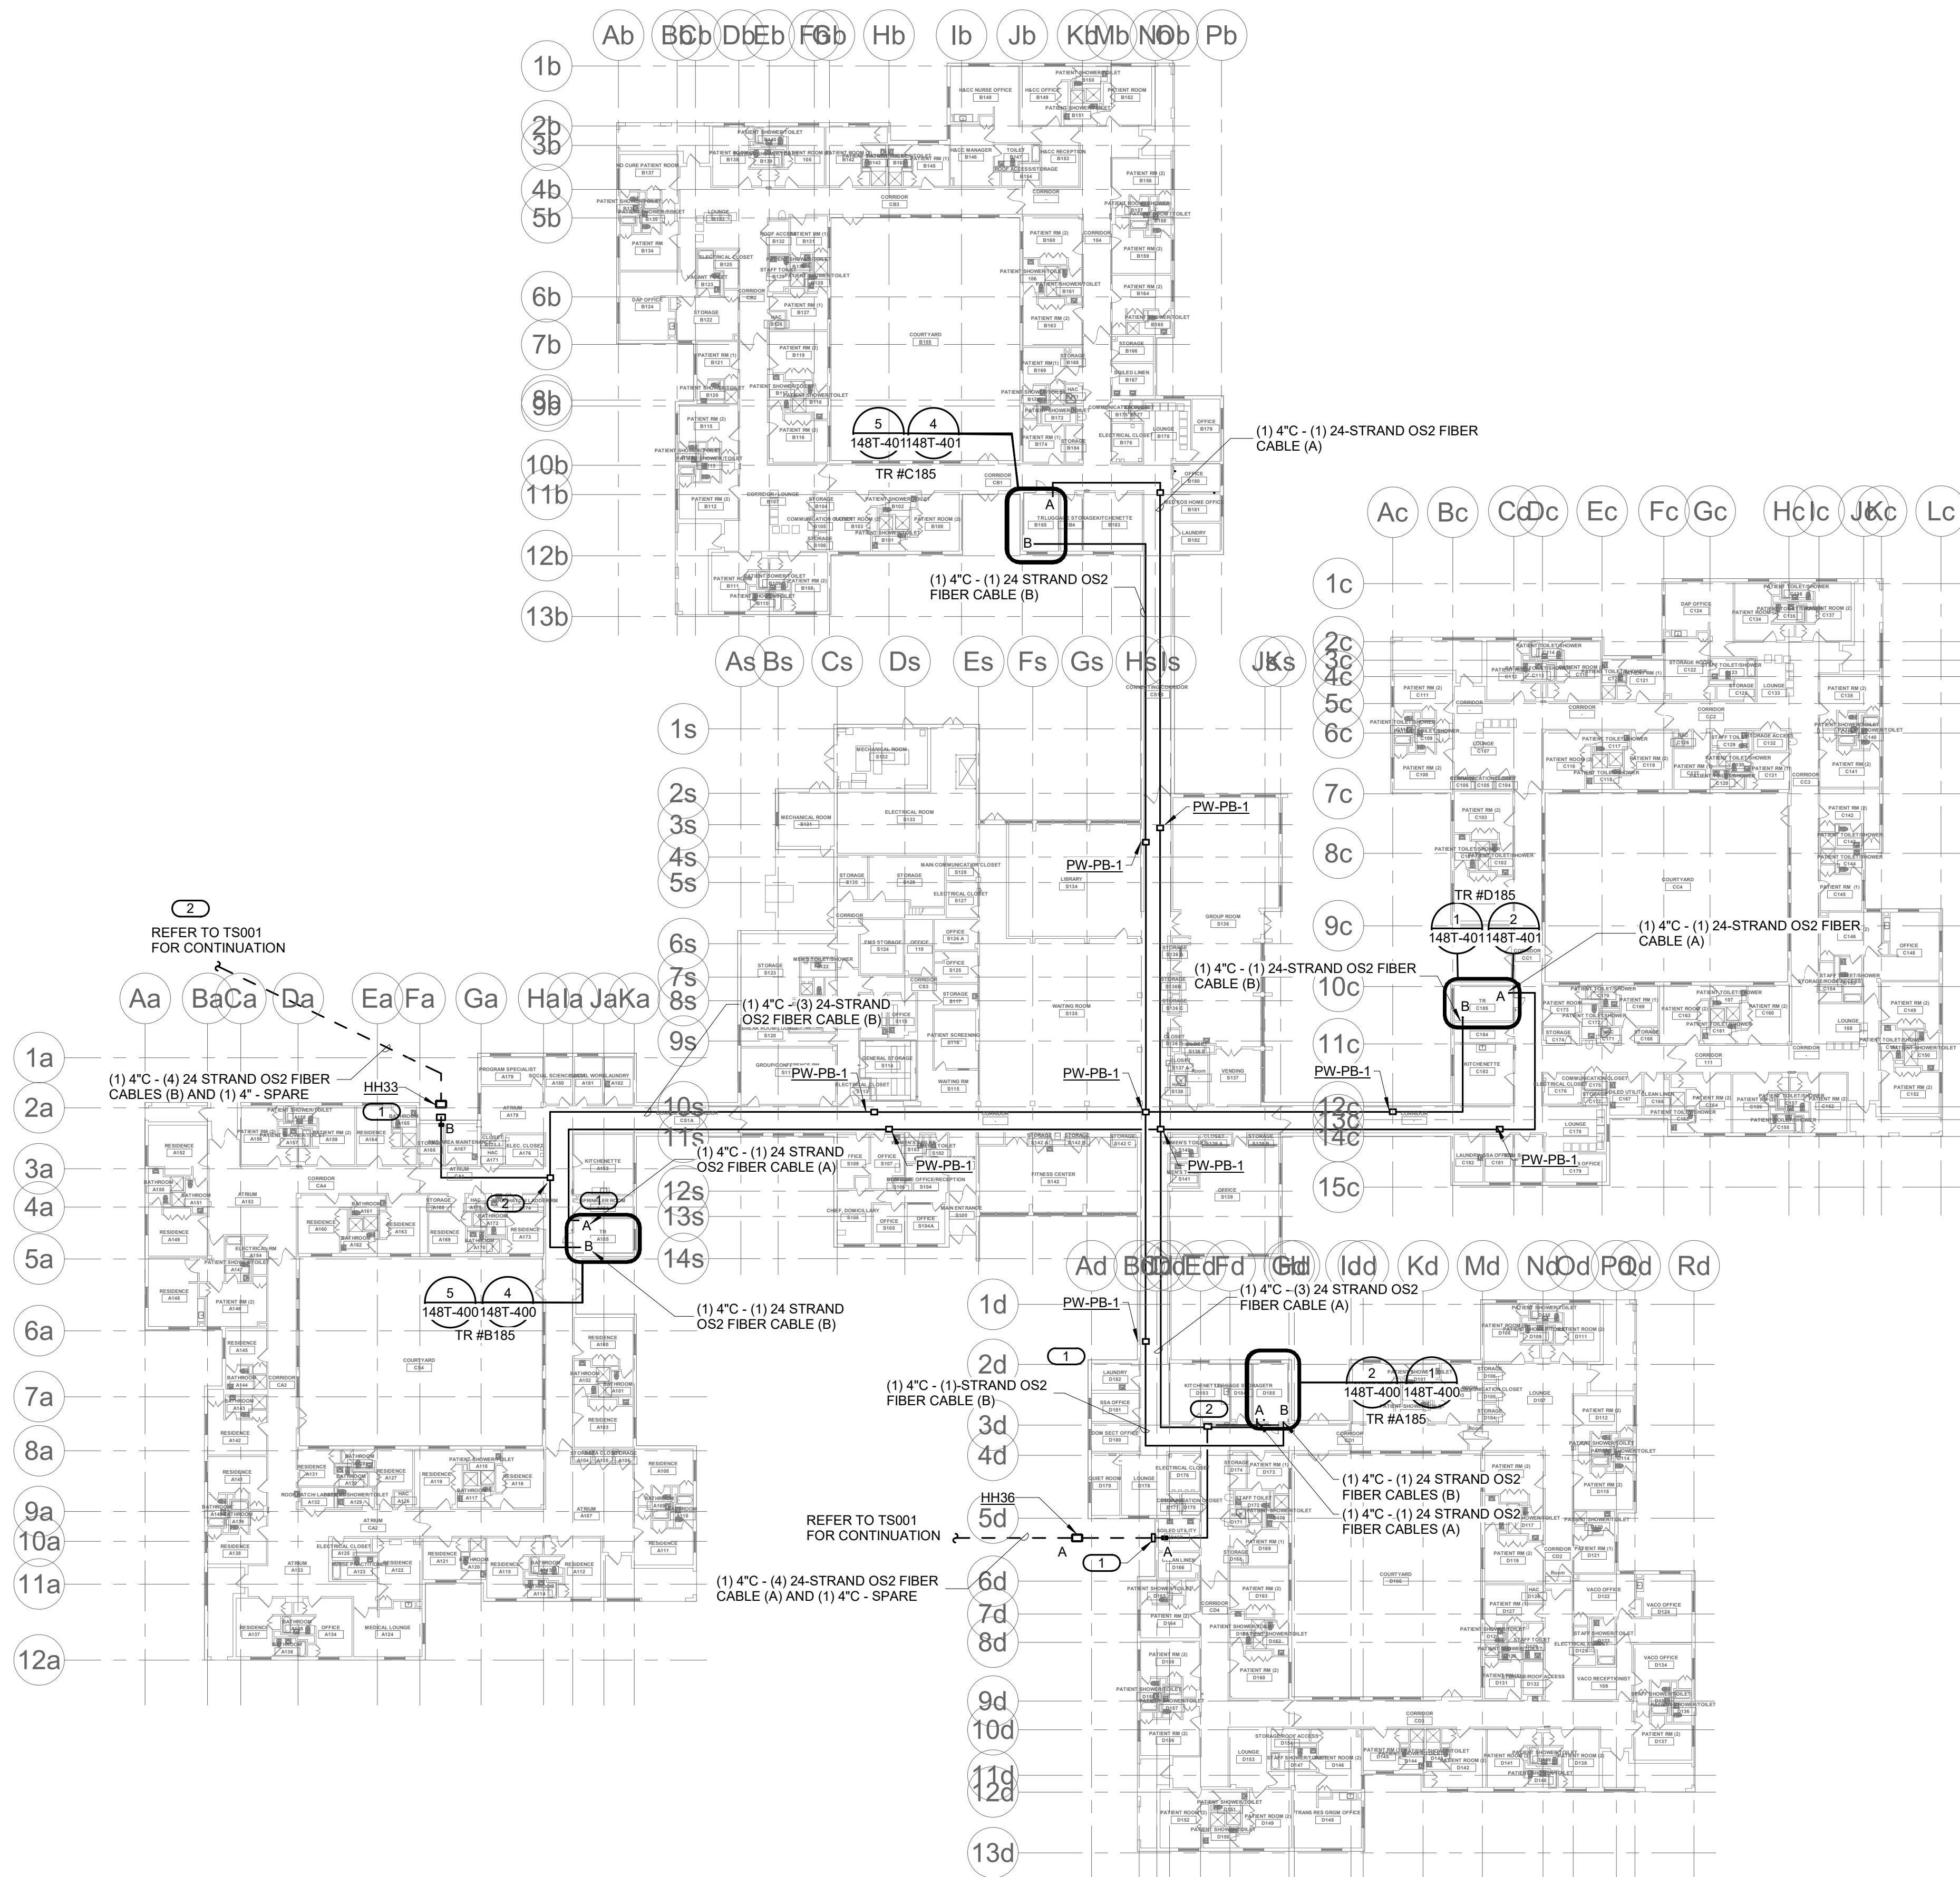

1 LEVEL 01 PLAN - TECHNOLOGY
1" = 30'-0"

--	--	

B:\M-360\509-22-700
VAHampton
E:\M-360\509-22-700\B148.T_R01.rvt


8/2/2025 8:35:52 AM

VA FORM 08 - 6231

Revisions:		Date:

CONSULTANT
ENGINEERING DISCIPLINE:
IMEG
www.imegcorp.com
225 W WASHINGTON STREET
SUITE 2700
CHICAGO, IL 60606
P: 312.294.0501 F: 312.294.0003
PROJECT #22010109.00

ARCHITECT/ENGINEER OF RECORD
A/E:
SPEES DESIGN BUILD
23830 PACIFIC HIGHWAY S. SUITE 203
KENT, WA 98032

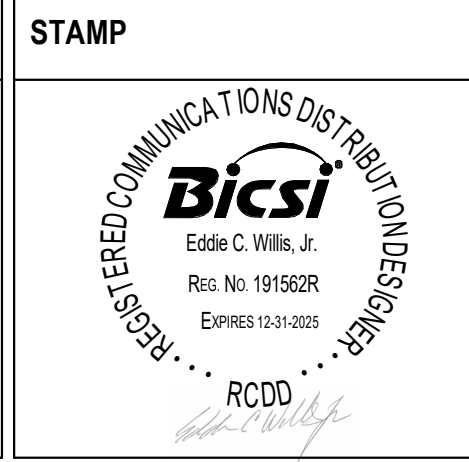


Office of
Construction
and Facilities
Management
VA U.S. Department
of Veterans Affairs

Drawing Title BLDG.148 TECHNOLOGY ENLARGED PLANS
Approved:

Phase 100% CONSTRUCTION DOCUMENTS
FULLY SPRINKLERED


Project Title EHRM INFRASTRUCTURE UPGRADES - HAMPTON
Location HAMPTON VA MEDICAL CENTER, HAMPTON, VIRGINIA
Issue Date 05/09/2025
Checked EW
Drawn IMEG

Project Number 509-22-700
Building Number 148
Drawing Number 148T-400
702 of 713

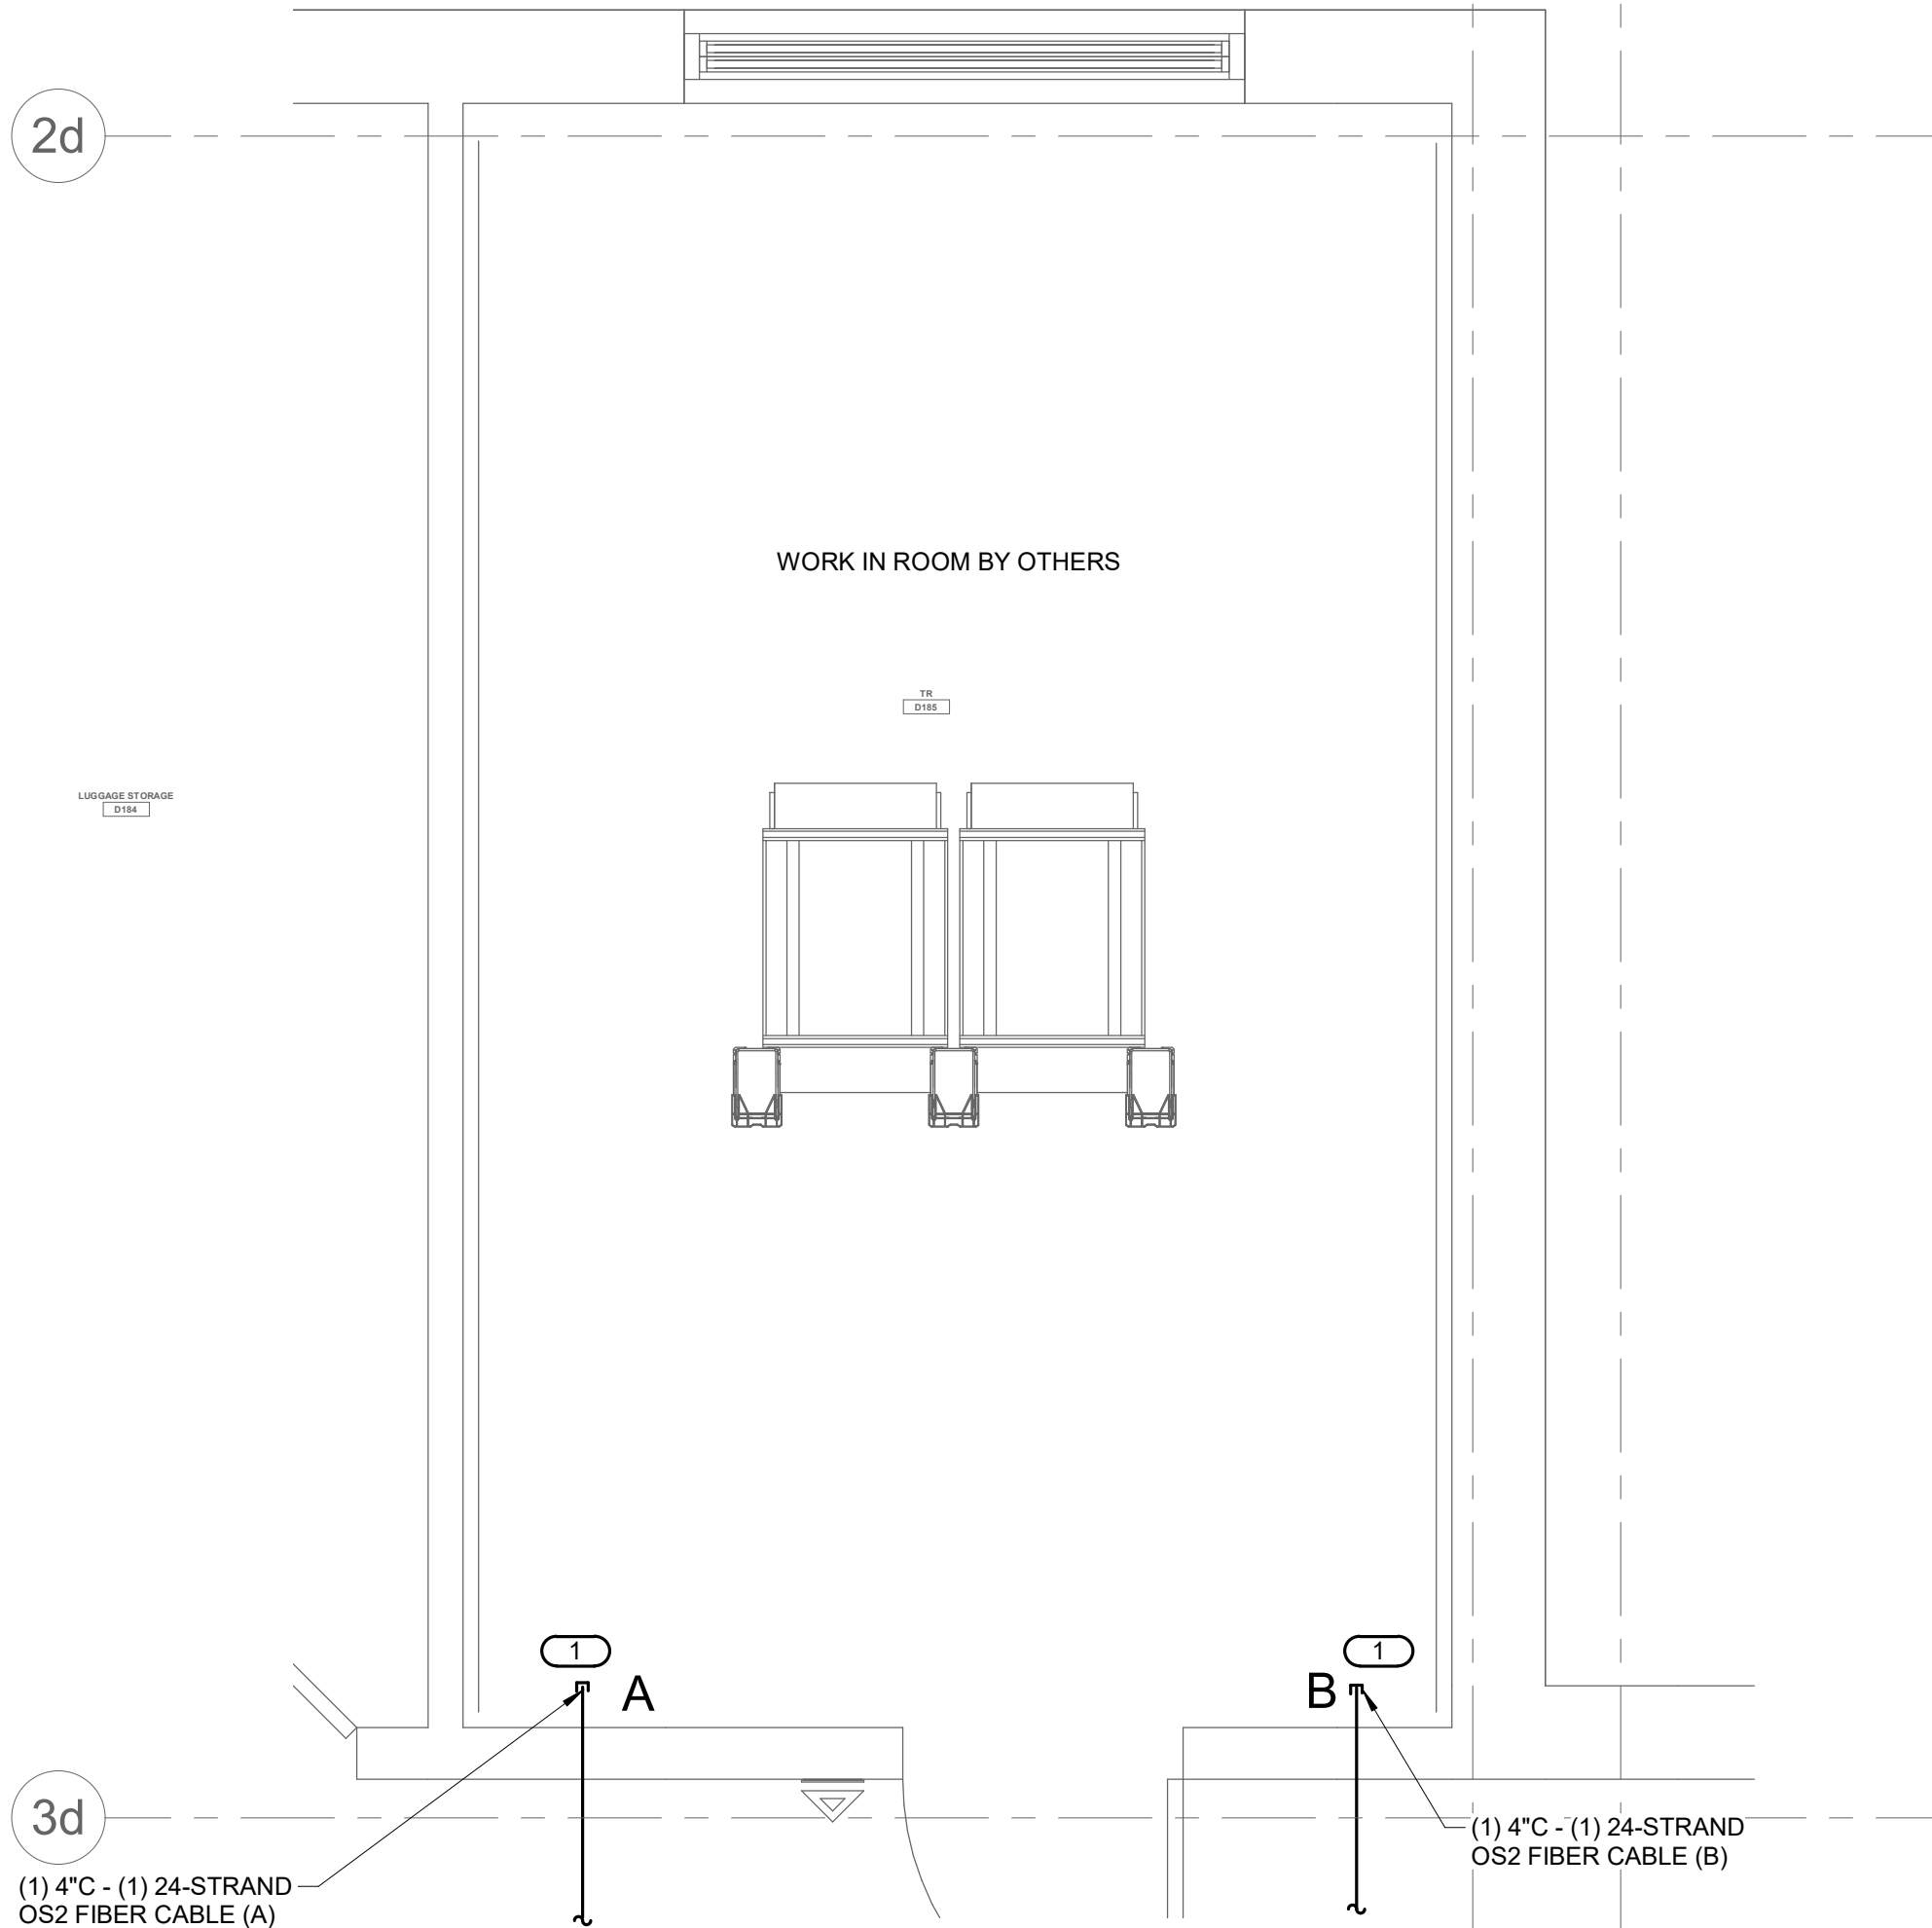


1 TELECOM ROOM ENLARGEMENT TR #A185
1/2" = 1'-0"
NOTES:
1. REFER TO ELECTRICAL DRAWINGS FOR ROOM LAYOUT AND RACK ELEVATIONS.
2. ROUTE OPTICAL FIBER CABLE TO OVERHEAD CABLE TRAY AND TERMINATE IN FIBER DISTRIBUTION CABINET.

KEY NOTES: **#**
1. THROUGH WALL PENETRATION FOR BACKBONE CONDUIT. OPTICAL FIBER CABLE CONTINUES ON CABLE TRAY TO RACKS.

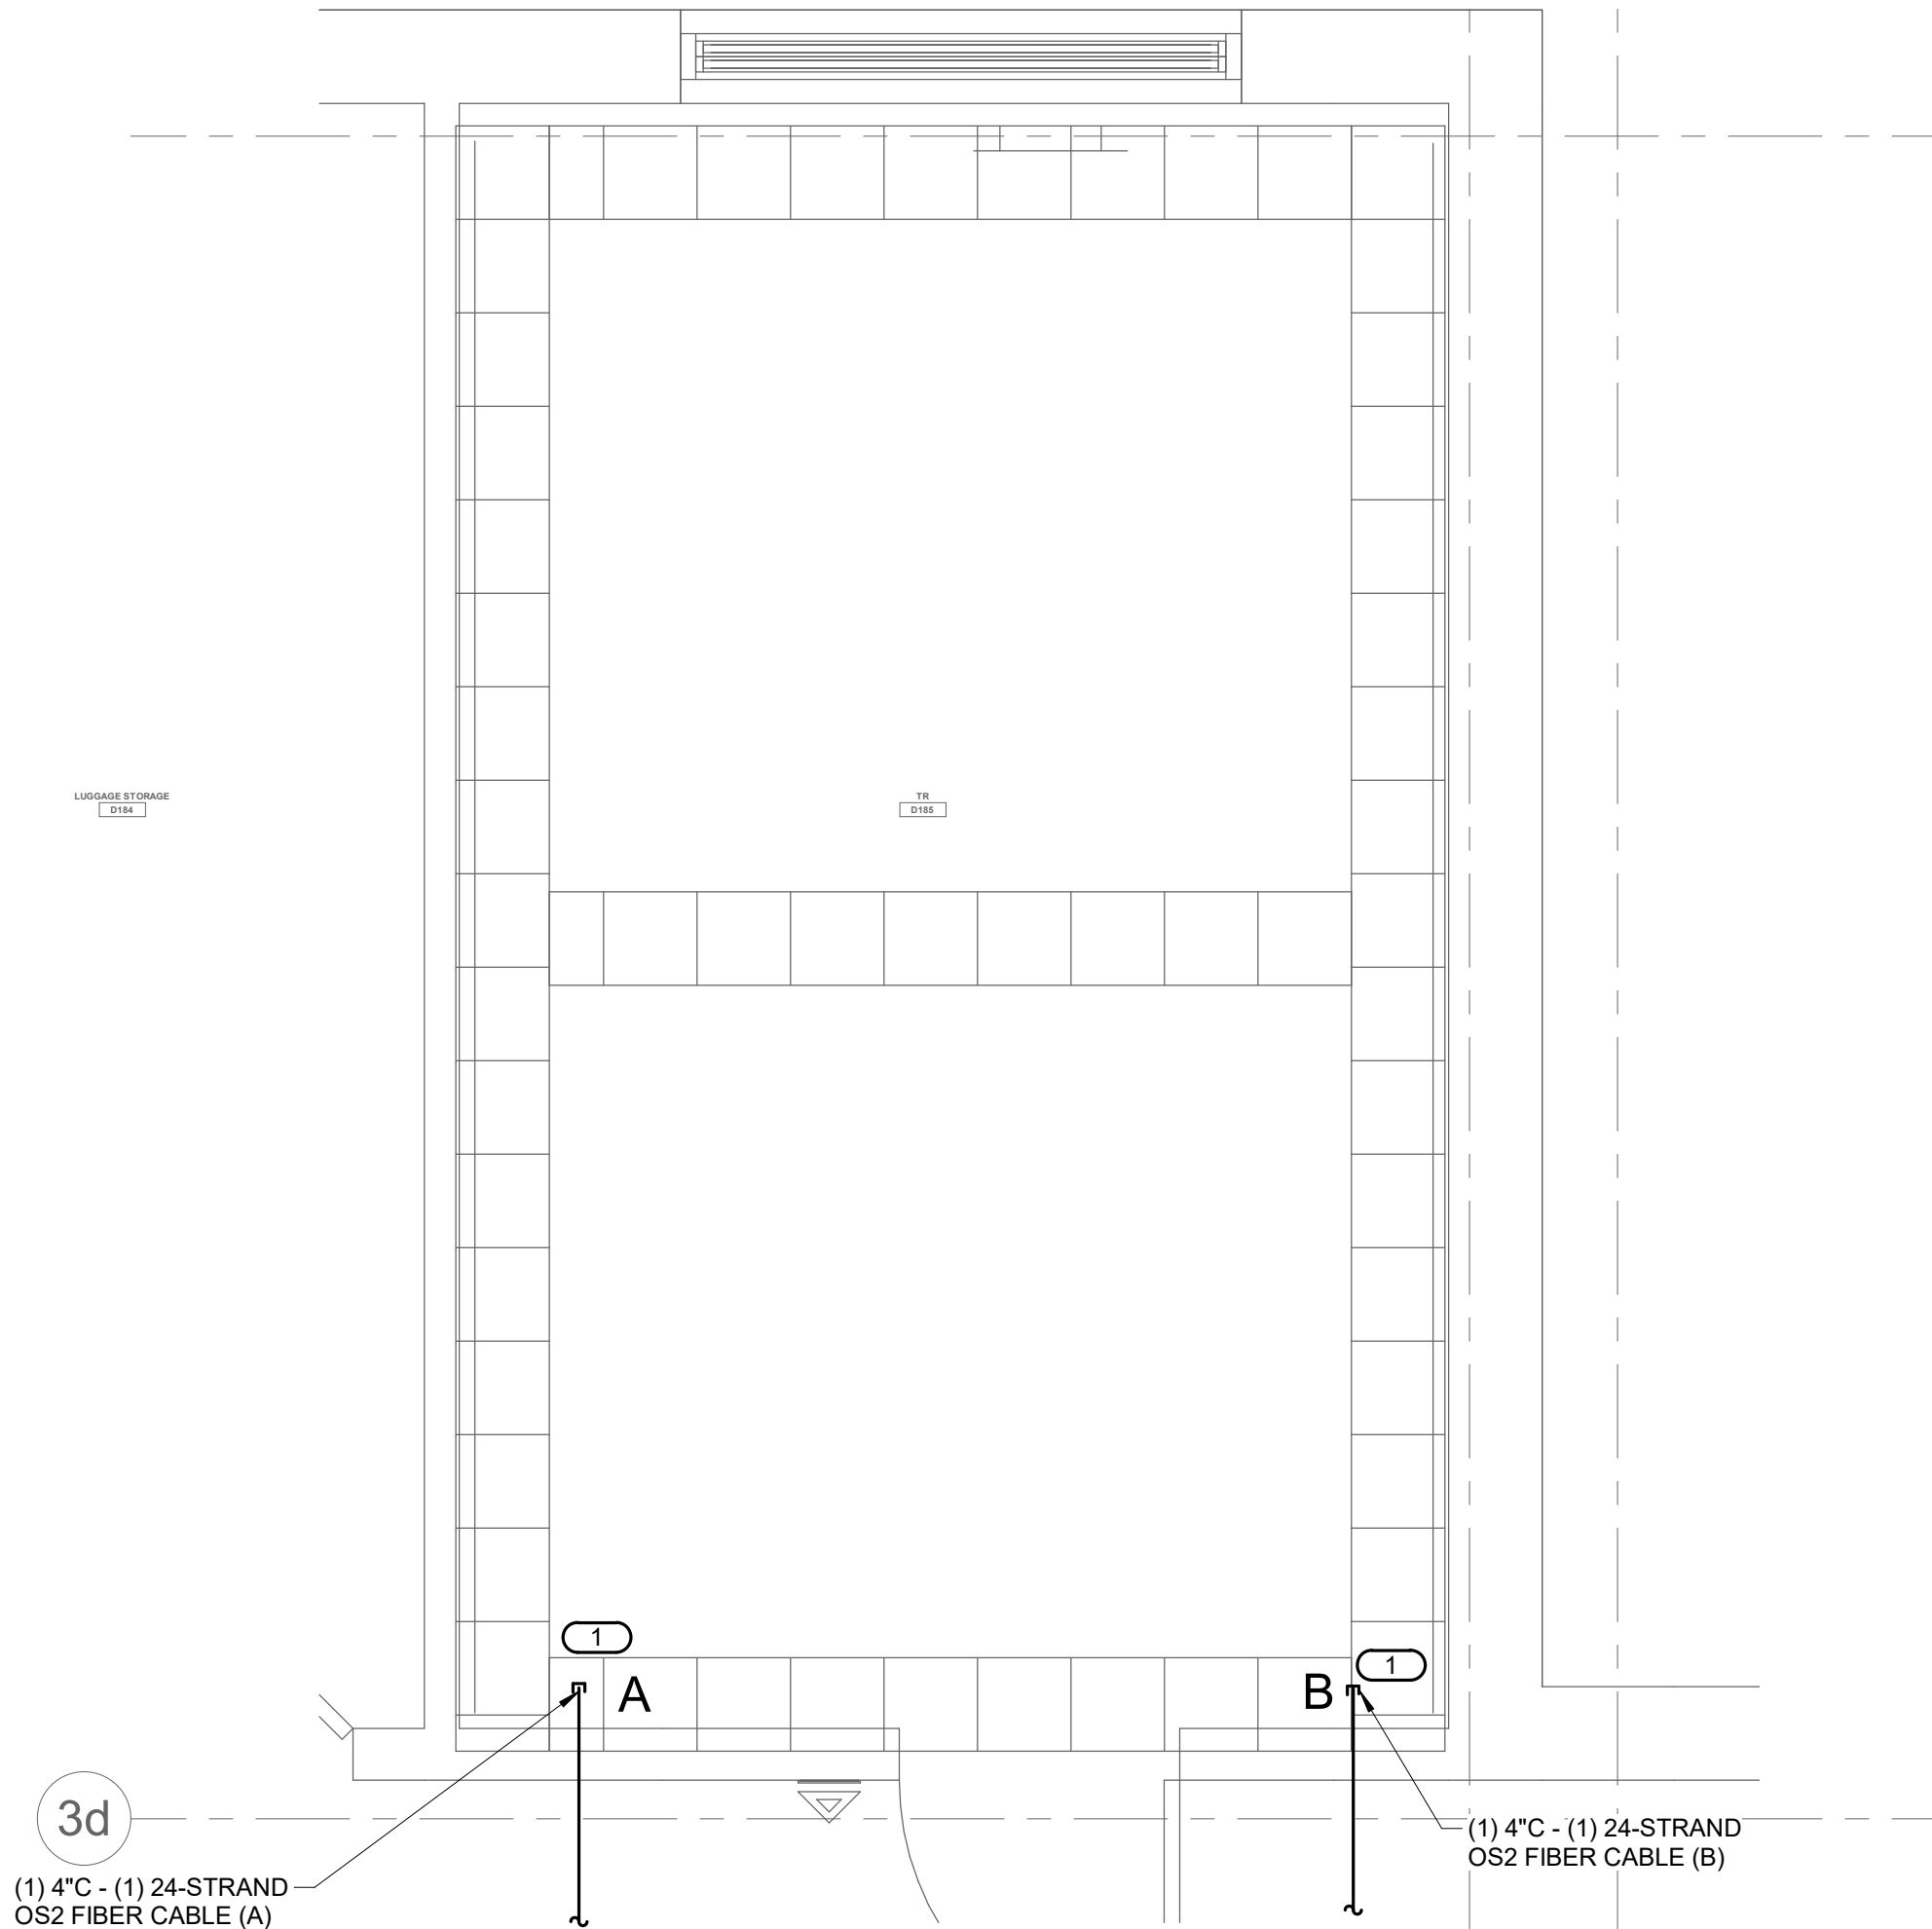


2 TELECOM ROOM PATHWAY TR #A185
1/2" = 1'-0"
NOTES:
1. REFER TO ELECTRICAL DRAWINGS FOR ROOM LAYOUT AND RACK ELEVATIONS.
2. ROUTE OPTICAL FIBER CABLE TO OVERHEAD CABLE TRAY AND TERMINATE IN FIBER DISTRIBUTION CABINET.

KEY NOTES: **#**
1. THROUGH WALL PENETRATION FOR BACKBONE CONDUIT. OPTICAL FIBER CABLE CONTINUES ON CABLE TRAY TO RACKS.

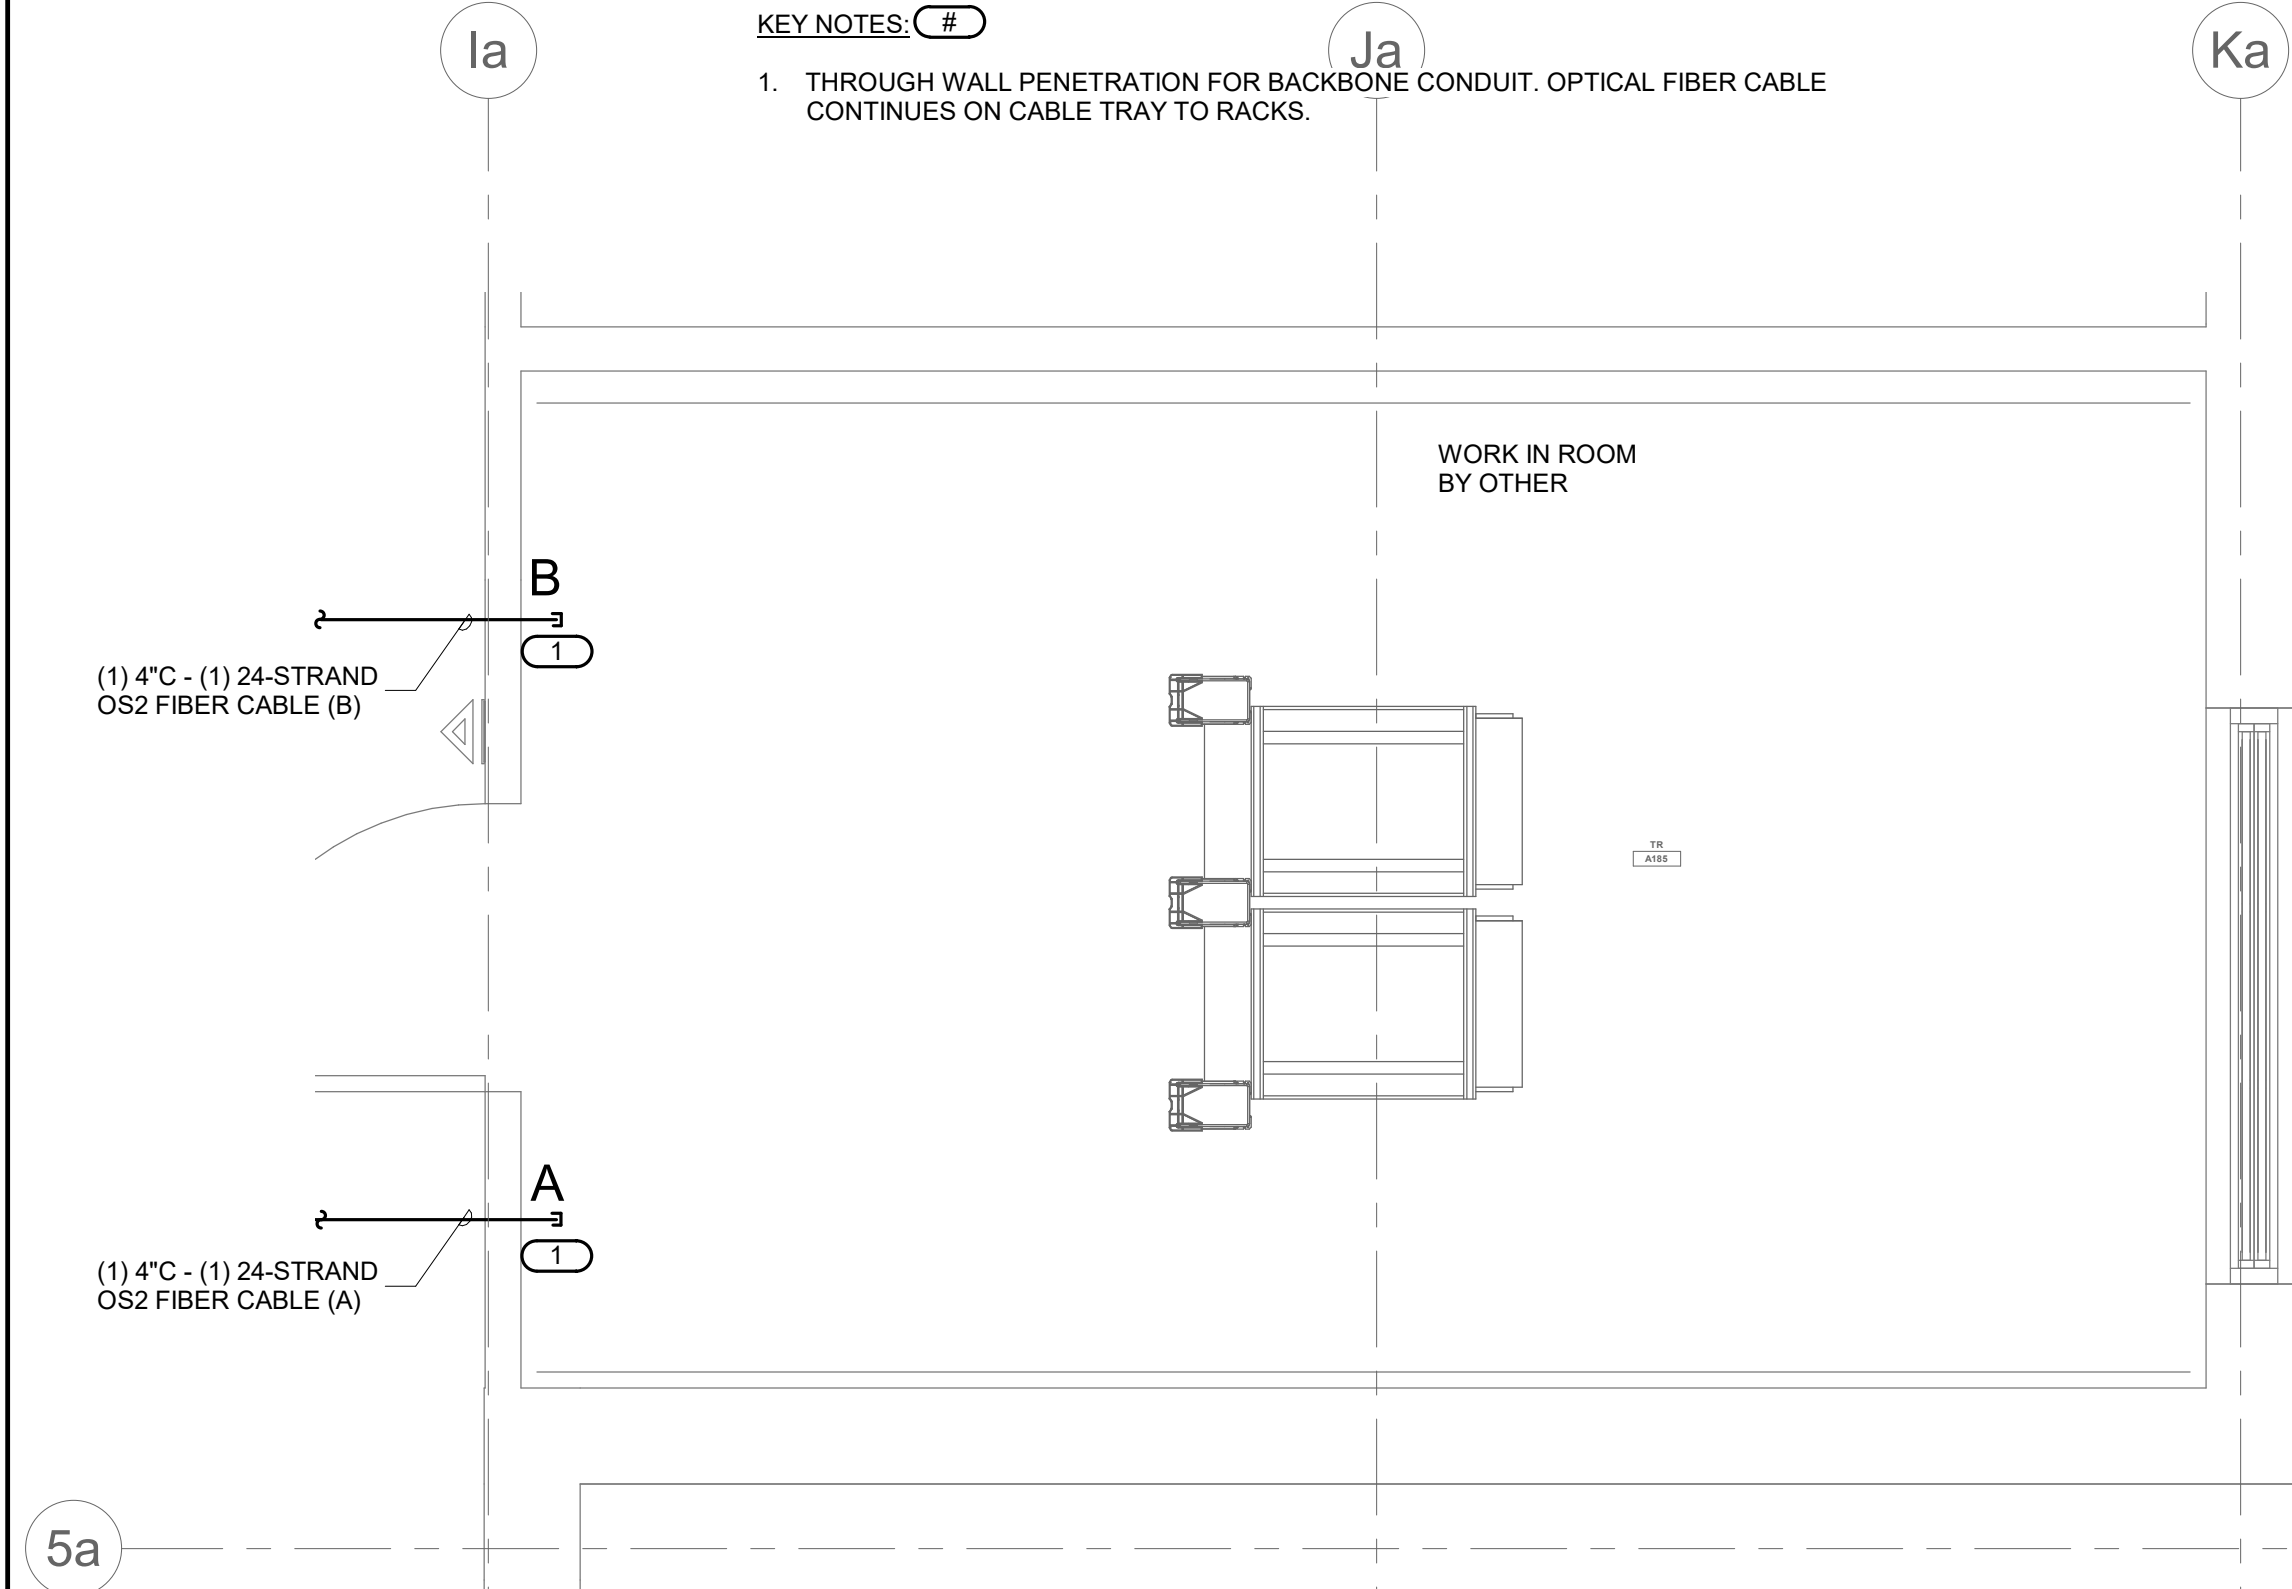

4 TELECOM ROOM ENLARGEMENT TR #B185
1/2" = 1'-0"
NOTES:
1. REFER TO ELECTRICAL DRAWINGS FOR ROOM LAYOUT AND RACK ELEVATIONS.
2. ROUTE OPTICAL FIBER CABLE TO OVERHEAD CABLE TRAY AND TERMINATE IN FIBER DISTRIBUTION CABINET.


KEY NOTES: **#**
1. THROUGH WALL PENETRATION FOR BACKBONE CONDUIT. OPTICAL FIBER CABLE CONTINUES ON CABLE TRAY TO RACKS.

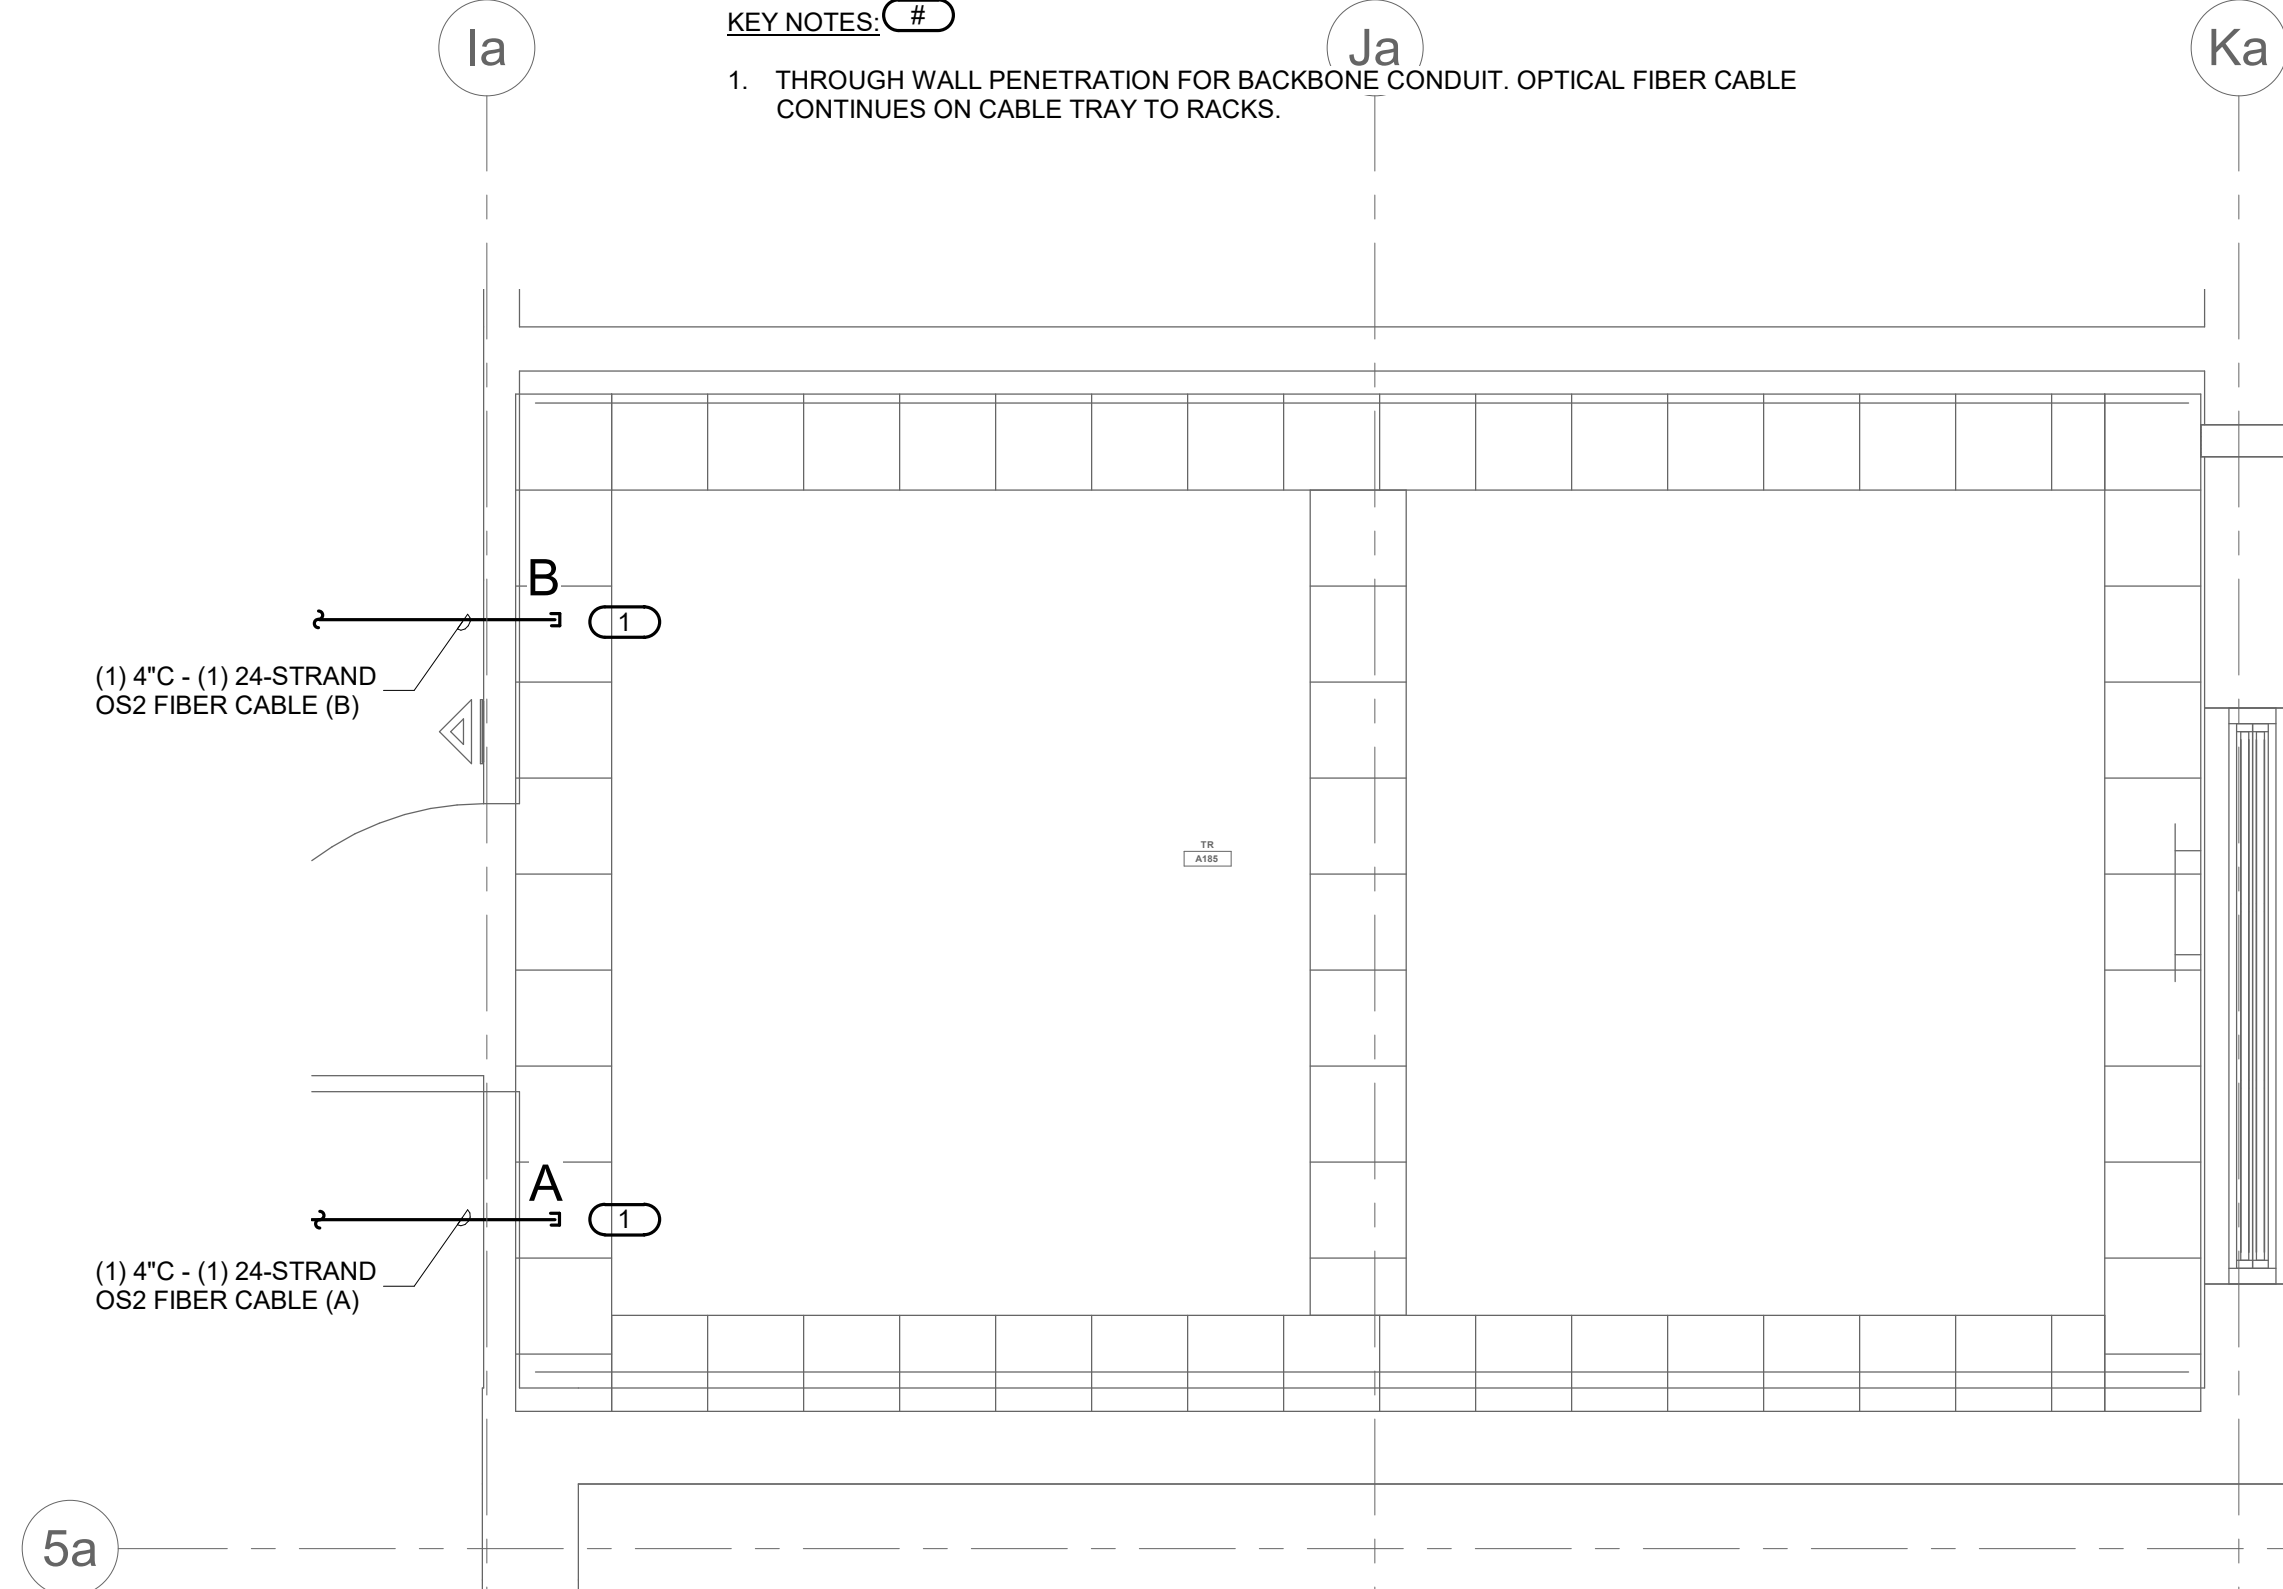

5 TELECOM ROOM PATHWAY TR #B185
1/2" = 1'-0"
NOTES:
1. REFER TO ELECTRICAL DRAWINGS FOR ROOM LAYOUT AND RACK ELEVATIONS.
2. ROUTE OPTICAL FIBER CABLE TO OVERHEAD CABLE TRAY AND TERMINATE IN FIBER DISTRIBUTION CABINET.


KEY NOTES: **#**
1. THROUGH WALL PENETRATION FOR BACKBONE CONDUIT. OPTICAL FIBER CABLE CONTINUES ON CABLE TRAY TO RACKS.

LEVEL 01

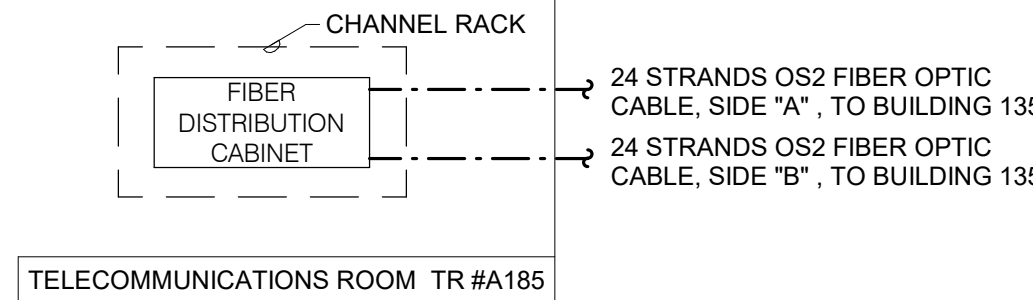

3 FIBER RISER DIAGRAM
NO SCALE
NOTES:
1. THIS RISER IS DIAGRAMMATIC AND MAY NOT SHOW ACTUAL ROUTING OR QUANTITIES OF MATERIALS SHOWN. THIS RISER IS SHOWN FOR CLARIFICATION OF CONNECTION(S), LOCATIONS AND CABLE TYPE. ALL INFORMATION OUTLETS ARE TYPICAL OF THE OUTLETS IN THE AREA SHOWN. REFER TO FLOOR PLANS FOR MORE SPECIFIC ROUTING INFORMATION. REFER TO SPECIFICATIONS FOR ADDITIONAL REQUIREMENTS.
2. REFER TO ELECTRICAL DRAWINGS FOR CHANNEL RACK AND FIBER OPTIC DISTRIBUTION CABINET SPECIFICATIONS

LEVEL 01

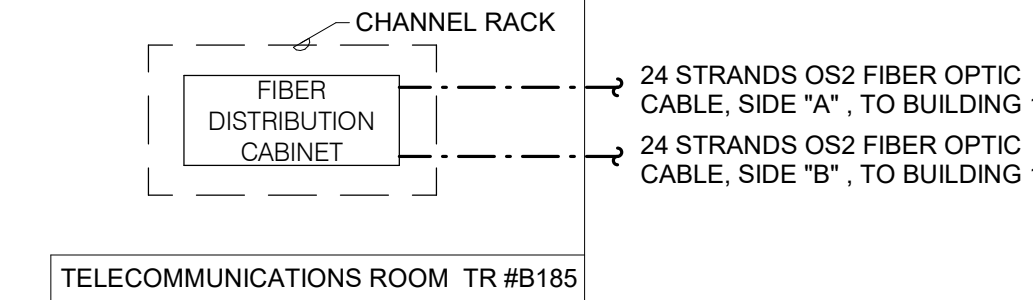

6 FIBER RISER DIAGRAM
NO SCALE
NOTES:
1. THIS RISER IS DIAGRAMMATIC AND MAY NOT SHOW ACTUAL ROUTING OR QUANTITIES OF MATERIALS SHOWN. THIS RISER IS SHOWN FOR CLARIFICATION OF CONNECTION(S), LOCATIONS AND CABLE TYPE. ALL INFORMATION OUTLETS ARE TYPICAL OF THE OUTLETS IN THE AREA SHOWN. REFER TO FLOOR PLANS FOR MORE SPECIFIC ROUTING INFORMATION. REFER TO SPECIFICATIONS FOR ADDITIONAL REQUIREMENTS.
2. REFER TO ELECTRICAL DRAWINGS FOR CHANNEL RACK AND FIBER OPTIC DISTRIBUTION CABINET SPECIFICATIONS

BIM 360://509-22-700
V:\Hampton
E:\148-700-B148-T_R1.rvt
8/21/2025 8:35:56 AM

VA FORM 08 - 6231



1

TELECOM ROOM ENLARGEMENT TR #C185

1/2" = 1'-0"


NOTES:

- REFER TO ELECTRICAL DRAWINGS FOR ROOM LAYOUT AND RACK ELEVATIONS.
- ROUTE OPTICAL FIBER CABLE TO OVERHEAD CABLE TRAY AND TERMINATE IN FIBER DISTRIBUTION CABINET.

(Jb)

KEY NOTES: (F)

- THROUGH WALL PENETRATION FOR BACKBONE CONDUIT. OPTICAL FIBER CABLE CONTINUES ON CABLE TRAY TO RACKS.

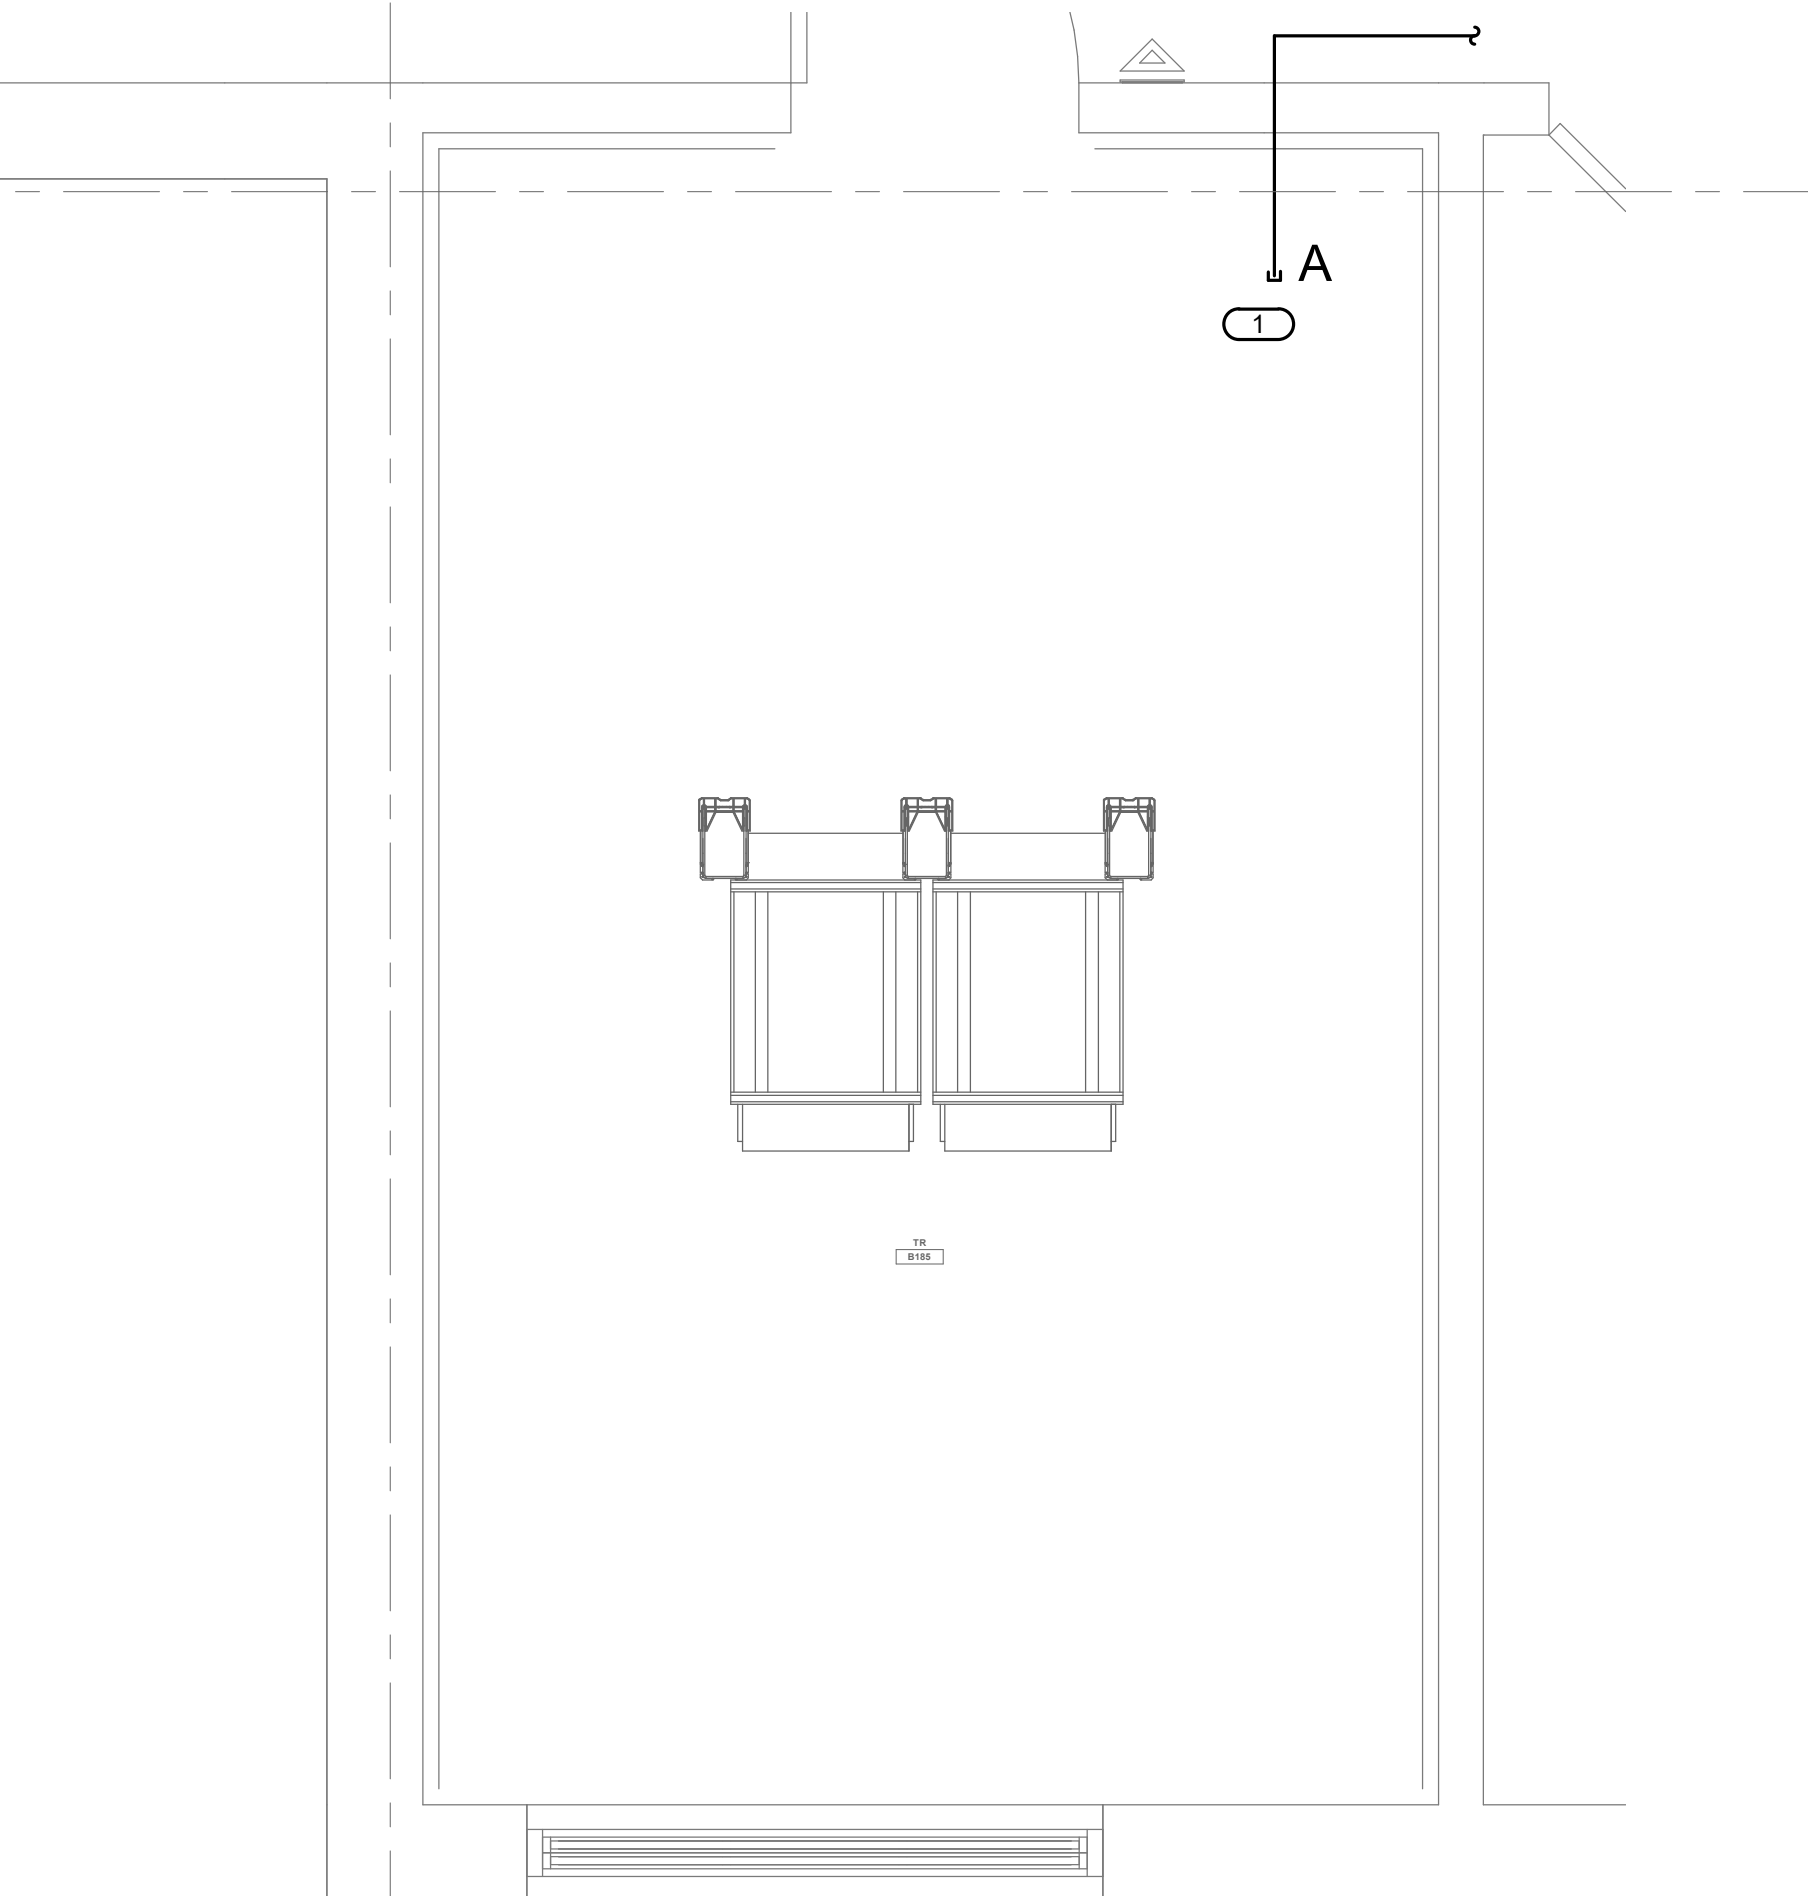

4

TELECOM ROOM ENLARGEMENT TR #D185

1/2" = 1'-0"

NOTES:

- REFER TO ELECTRICAL DRAWINGS FOR ROOM LAYOUT AND RACK ELEVATIONS.
- ROUTE OPTICAL FIBER CABLE TO OVERHEAD CABLE TRAY AND TERMINATE IN FIBER DISTRIBUTION CABINET.

KEY NOTES: (F)

- THROUGH WALL PENETRATION FOR BACKBONE CONDUIT. OPTICAL FIBER CABLE CONTINUES ON CABLE TRAY TO RACKS.



2

TELECOM ROOM PATHWAY TR #C185

1/2" = 1'-0"


NOTES:

- REFER TO ELECTRICAL DRAWINGS FOR ROOM LAYOUT AND RACK ELEVATIONS.
- ROUTE OPTICAL FIBER CABLE TO OVERHEAD CABLE TRAY AND TERMINATE IN FIBER DISTRIBUTION CABINET.

(Jb)

KEY NOTES: (F)

- THROUGH WALL PENETRATION FOR BACKBONE CONDUIT. OPTICAL FIBER CABLE CONTINUES ON CABLE TRAY TO RACKS.

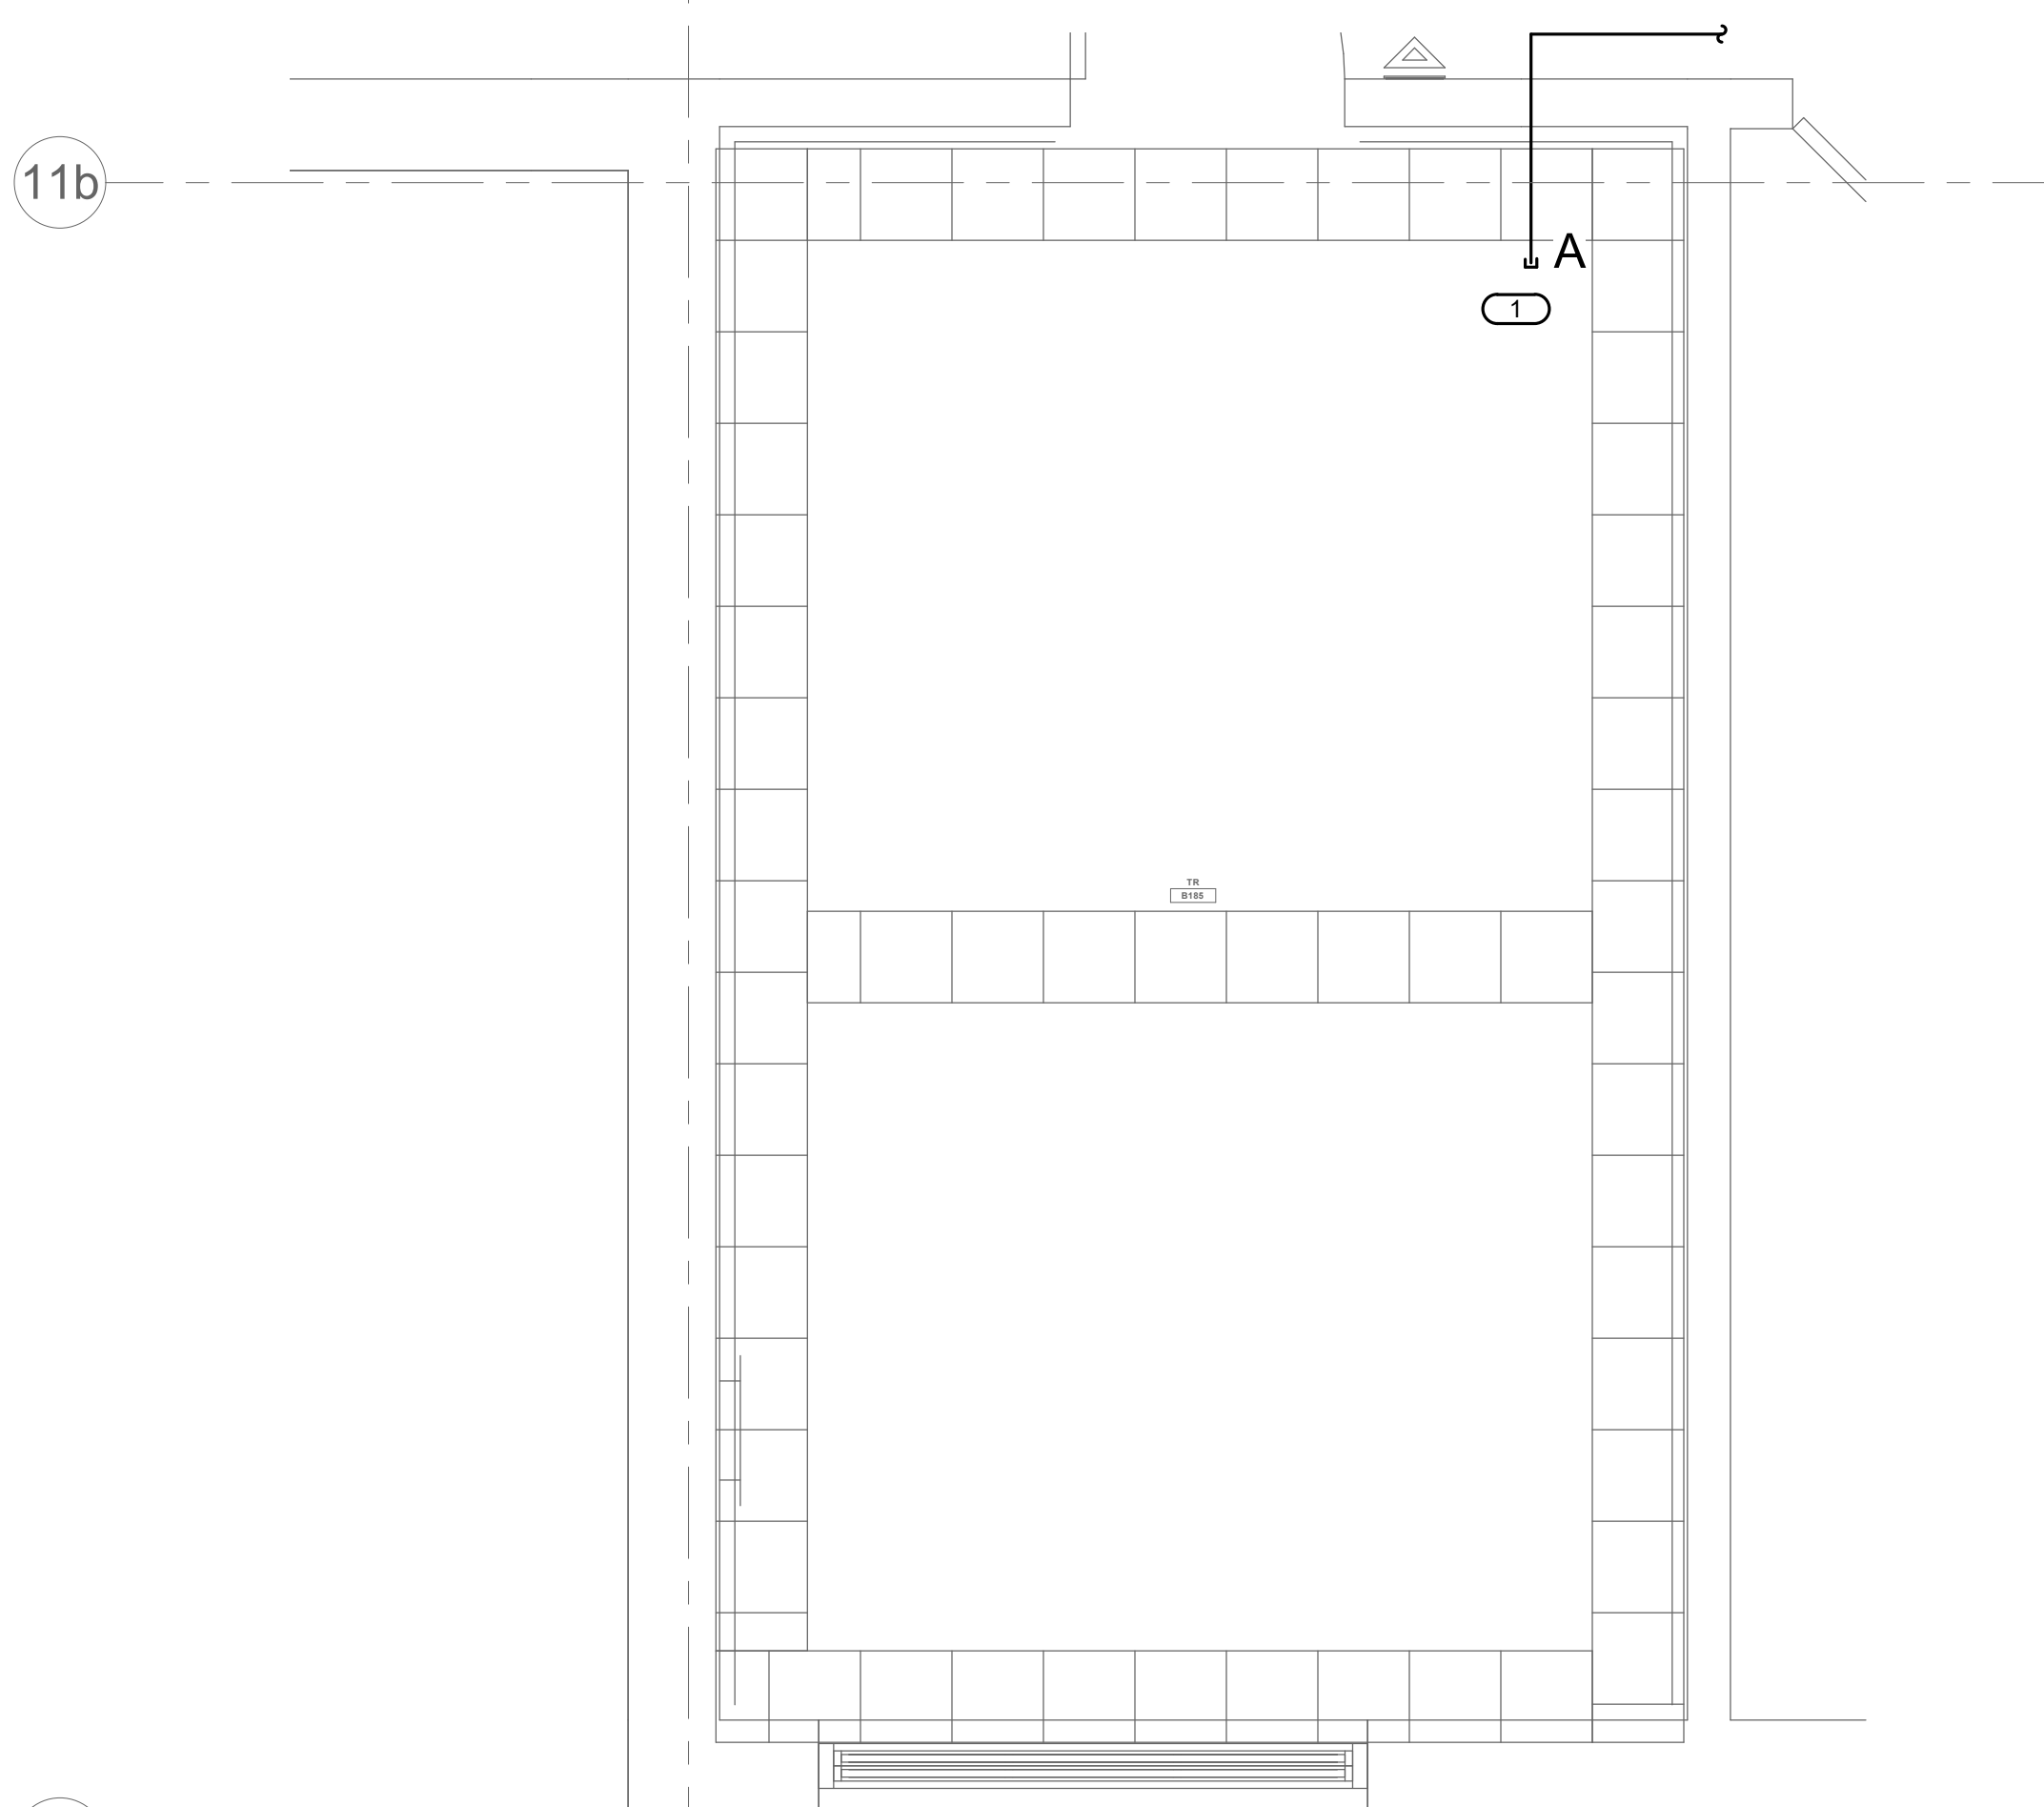

5

TELECOM ROOM PATHWAY TR #D185

1/2" = 1'-0"


NOTES:

- REFER TO ELECTRICAL DRAWINGS FOR ROOM LAYOUT AND RACK ELEVATIONS.
- ROUTE OPTICAL FIBER CABLE TO OVERHEAD CABLE TRAY AND TERMINATE IN FIBER DISTRIBUTION CABINET.

KEY NOTES: (F)

- THROUGH WALL PENETRATION FOR BACKBONE CONDUIT. OPTICAL FIBER CABLE CONTINUES ON CABLE TRAY TO RACKS.

LEVEL 01

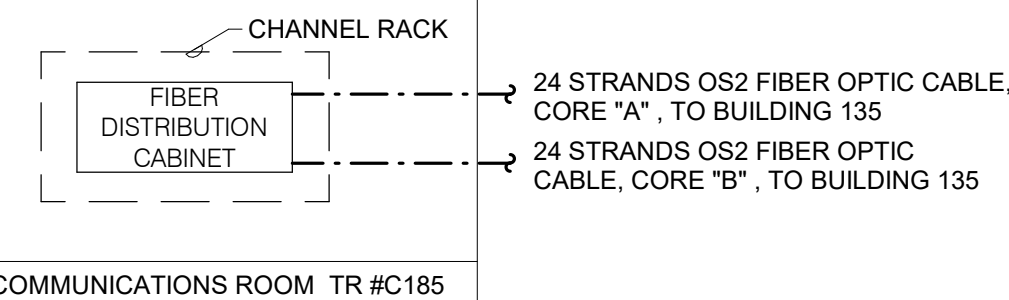

3


FIBER RISER DIAGRAM

NO SCALE

NOTES:

- THIS RISER IS DIAGRAMMATIC AND MAY NOT SHOW ACTUAL ROUTING OR QUANTITIES OF MATERIALS SHOWN. THIS RISER IS SHOWN FOR CLARIFICATION OF CONNECTION(S), LOCATIONS AND CABLE TYPE. ALL INFORMATION OUTLETS ARE TYPICAL OF THE OUTLETS IN THE AREA SHOWN. REFER TO FLOOR PLANS FOR MORE SPECIFIC ROUTING INFORMATION. REFER TO SPECIFICATIONS FOR ADDITIONAL REQUIREMENTS.
- REFER TO ELECTRICAL DRAWINGS FOR CHANNEL RACK AND FIBER OPTIC DISTRIBUTION CABINET SPECIFICATIONS

LEVEL 01

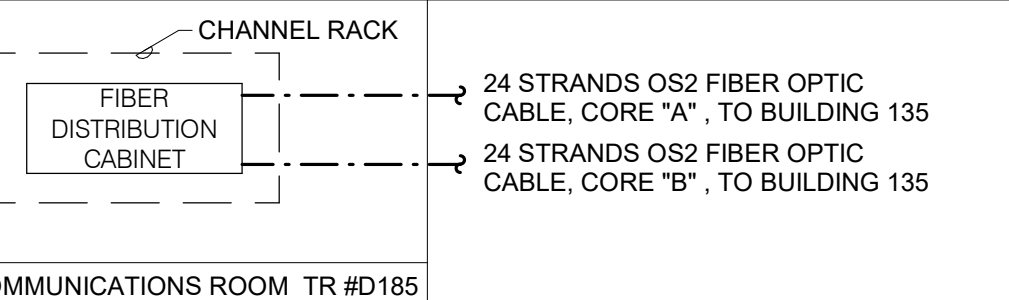

6

FIBER RISER DIAGRAM

NO SCALE


NOTES:

- THIS RISER IS DIAGRAMMATIC AND MAY NOT SHOW ACTUAL ROUTING OR QUANTITIES OF MATERIALS SHOWN. THIS RISER IS SHOWN FOR CLARIFICATION OF CONNECTION(S), LOCATIONS AND CABLE TYPE. ALL INFORMATION OUTLETS ARE TYPICAL OF THE OUTLETS IN THE AREA SHOWN. REFER TO FLOOR PLANS FOR MORE SPECIFIC ROUTING INFORMATION. REFER TO SPECIFICATIONS FOR ADDITIONAL REQUIREMENTS.
- REFER TO ELECTRICAL DRAWINGS FOR CHANNEL RACK AND FIBER OPTIC DISTRIBUTION CABINET SPECIFICATIONS

Revisions:	Date:

CONSULTANT
ENGINEERING DISCIPLINE:
IMEG
www.imegcorp.com
225 W WASHINGTON STREET
SUITE 2700
CHICAGO, IL 60606
P: 312.294.0501 F: 312.294.0003
PROJECT #22010109.00

ARCHITECT/ENGINEER OF RECORD
A/E:
SPEES DESIGN BUILD
23830 PACIFIC HIGHWAY S. SUITE 203
KENT, WA 98032

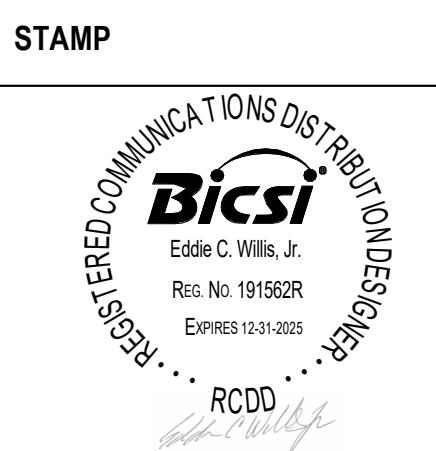

Office of
Construction
and Facilities
Management
VA U.S. Department
of Veterans Affairs

Drawing Title
BLDG.148 TECHNOLOGY ENLARGED PLANS
Approved:

Phase
100% CONSTRUCTION
DOCUMENTS
FULLY SPRINKLERED

Project Title
EHRM INFRASTRUCTURE
UPGRADES - HAMPTON

Location
HAMPTON VA MEDICAL CENTER, HAMPTON, VIRGINIA

Issue Date
05/09/2025

Checked
EW

Drawn
IMEG

Project Number
509-22-700
Building Number
148
Drawing Number
148T-401
703 of 713

- SHEET NOTES:
1. REFER TO SITE PLAN TS001 FOR ADDITIONAL INFORMATION.

2. REFER TO TS00 AND TS01 FOR CAMPUS OPTICAL FIBER CABLE RISER DIAGRAMS.

3. REFER TO 217400 FOR HANDHOLE DETAIL.


4. NEW BACKBONE OPTICAL FIBER CABLES SHALL BE INDOOR/OUTDOOR TYPE.

5. ALL BACKBONE OPTICAL FIBER CABLE PATHWAYS SHALL BE NEW. DO NOT RE-USE EXISTING BACKBONE CABLE PATHWAYS FOR NEW BACKBONE CABLES.

6. TRANSITION PVC CONDUITS TO GRC IN CRAWL SPACE OR EXPOSED EXTERIOR LOCATIONS. TRANSITION TO EMT CONDUITS AT INTERIOR OF BUILDING SEAL ALL PENETRATIONS TO MAINTAIN FIRE-RATINGS OF WALL, CEILING AND FLOORS.

7. CONDUIT ROUTES THRU CRAWL SPACE ARE "SUGGESTED" ROUTE. FIELD VERIFY EXACT ROUTE THRU CRAWL SPACE.
- KEY NOTES:

#
1. PROVIDE PULLBOX ON EXTERIOR WALL AT HEIGHT ABOVE FINISHED CEILING. ROUTE CONDUIT UP WALL INTO PULLBOX. PROVIDE PENETRATION THRU WALL AND ROUTE CONDUIT THRU WALL ABOVE CEILING INTO TR #115.

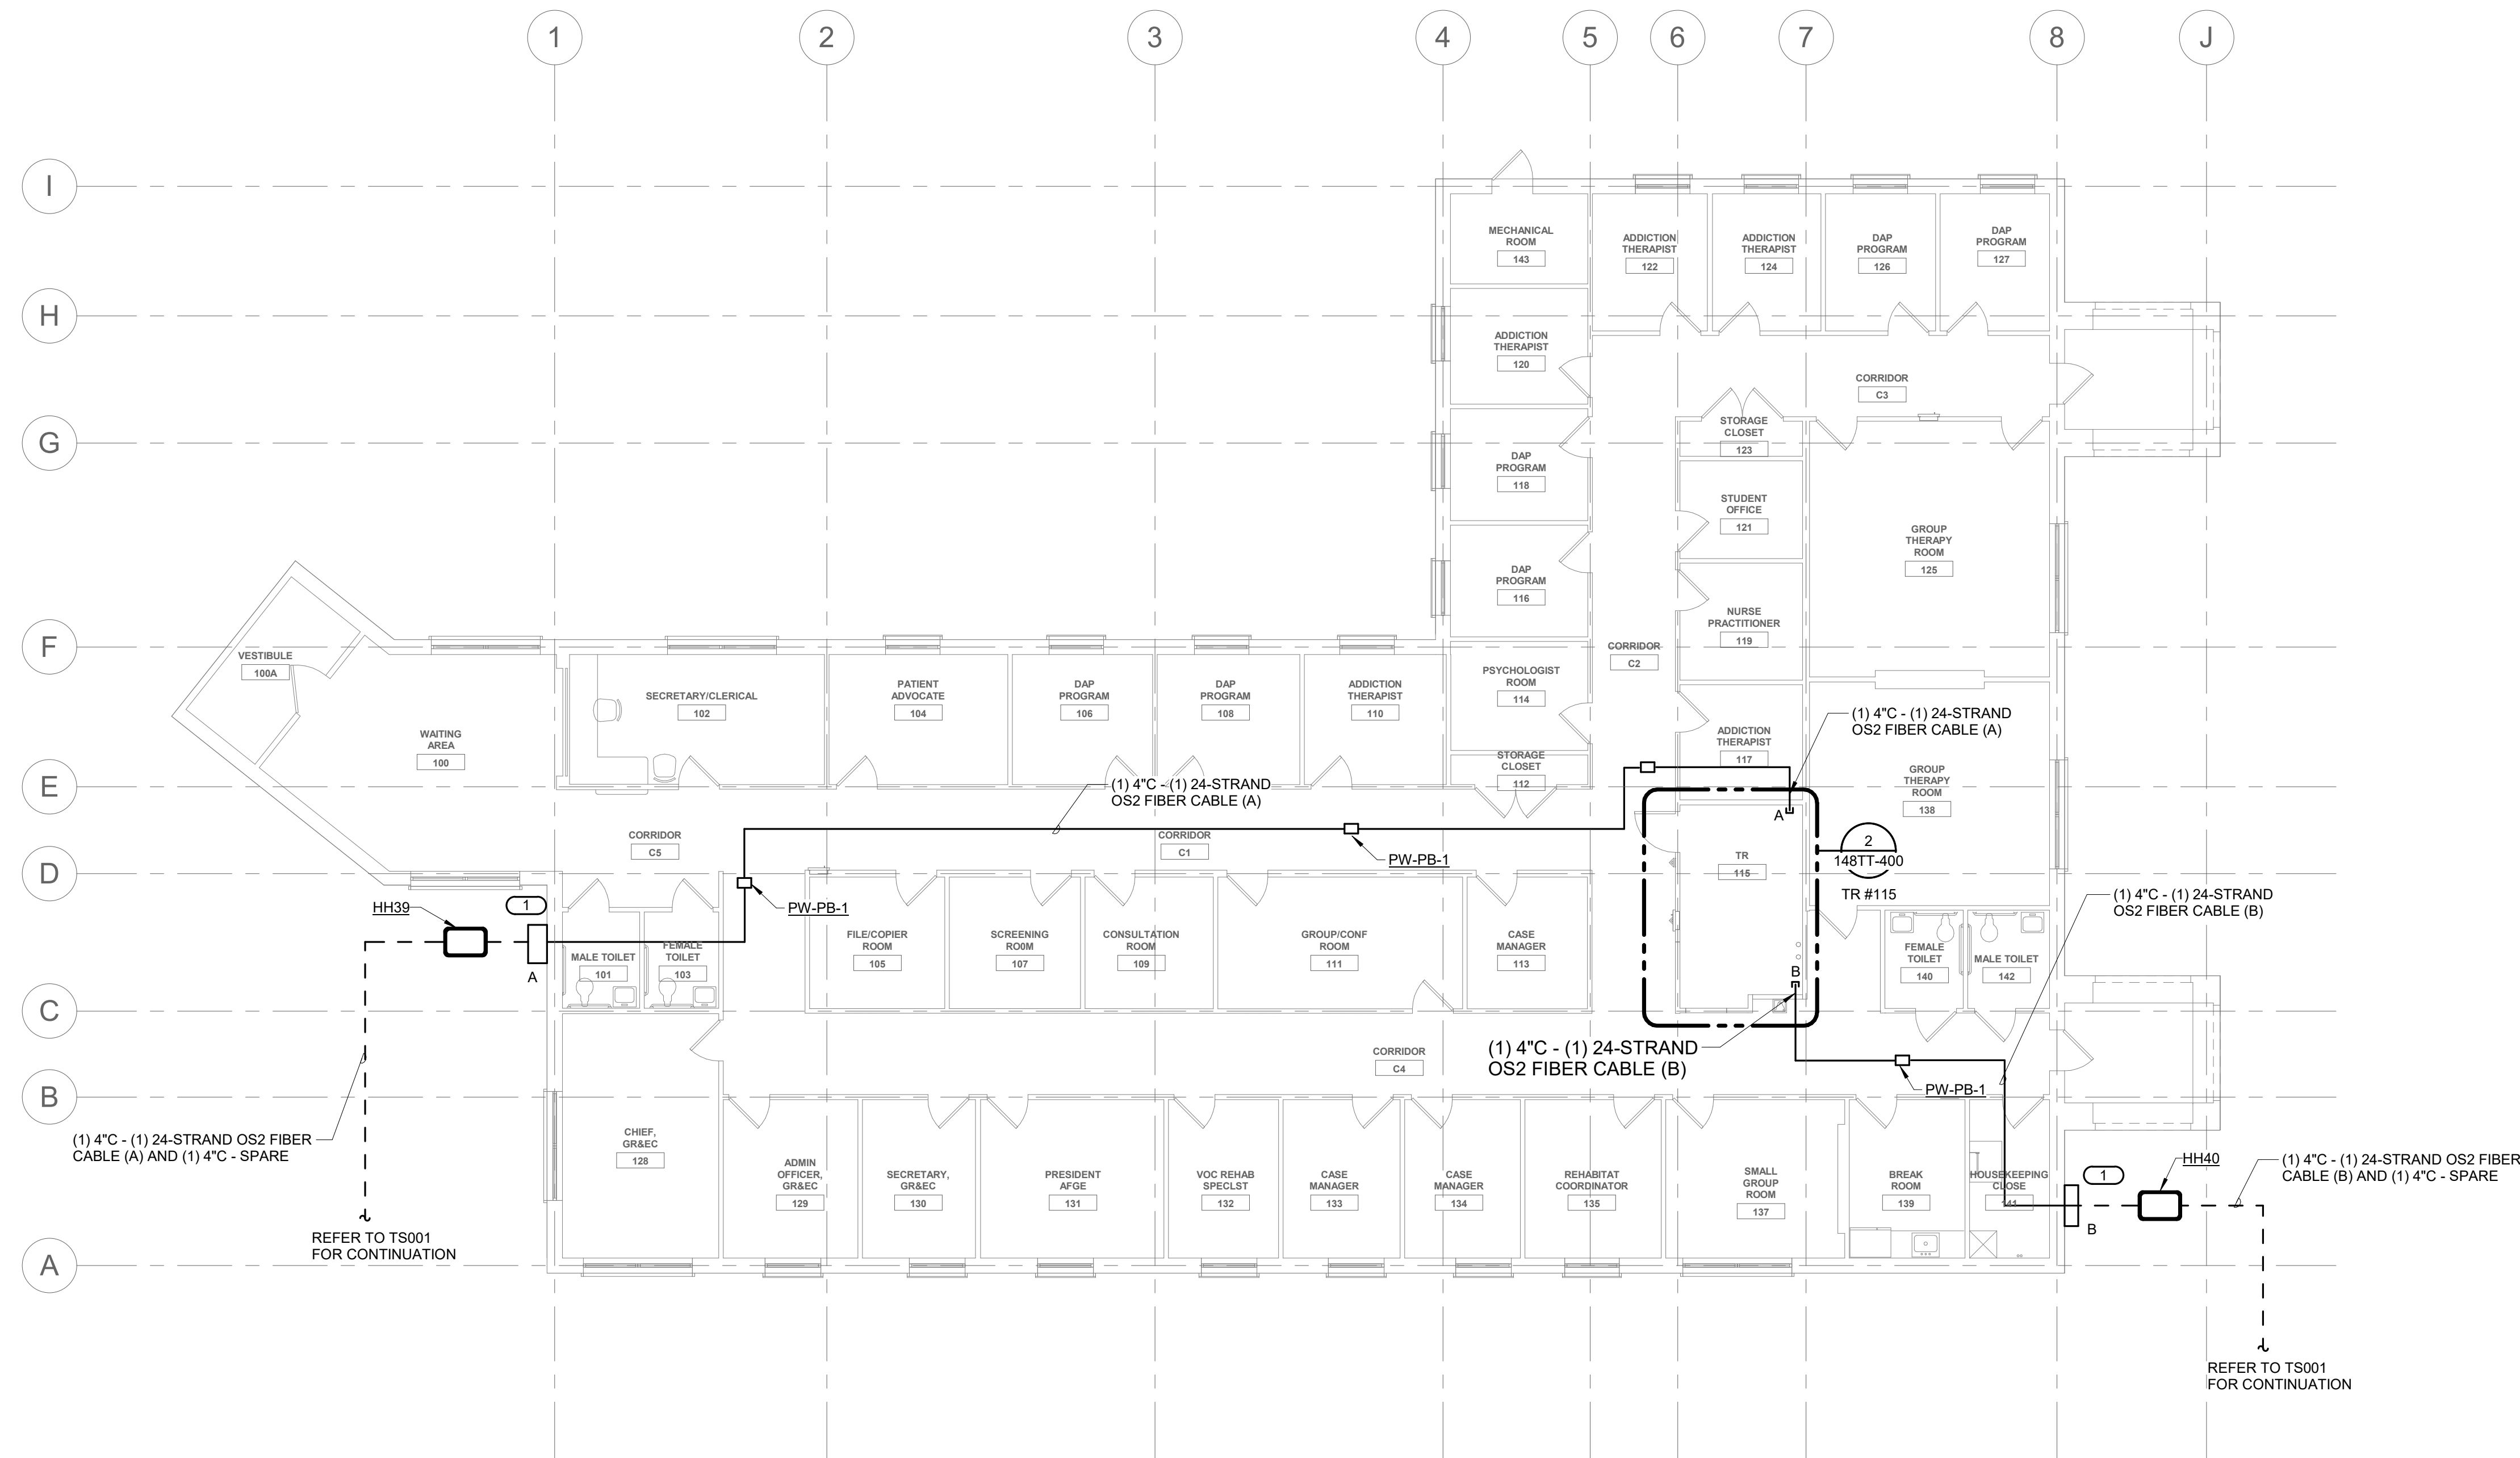

1


LEVEL 01 PLAN - TECHNOLOGY

1/8" = 1'-0"

	</
--	--	----


A
B
C
D
E
F

A
B
C
D
E
F

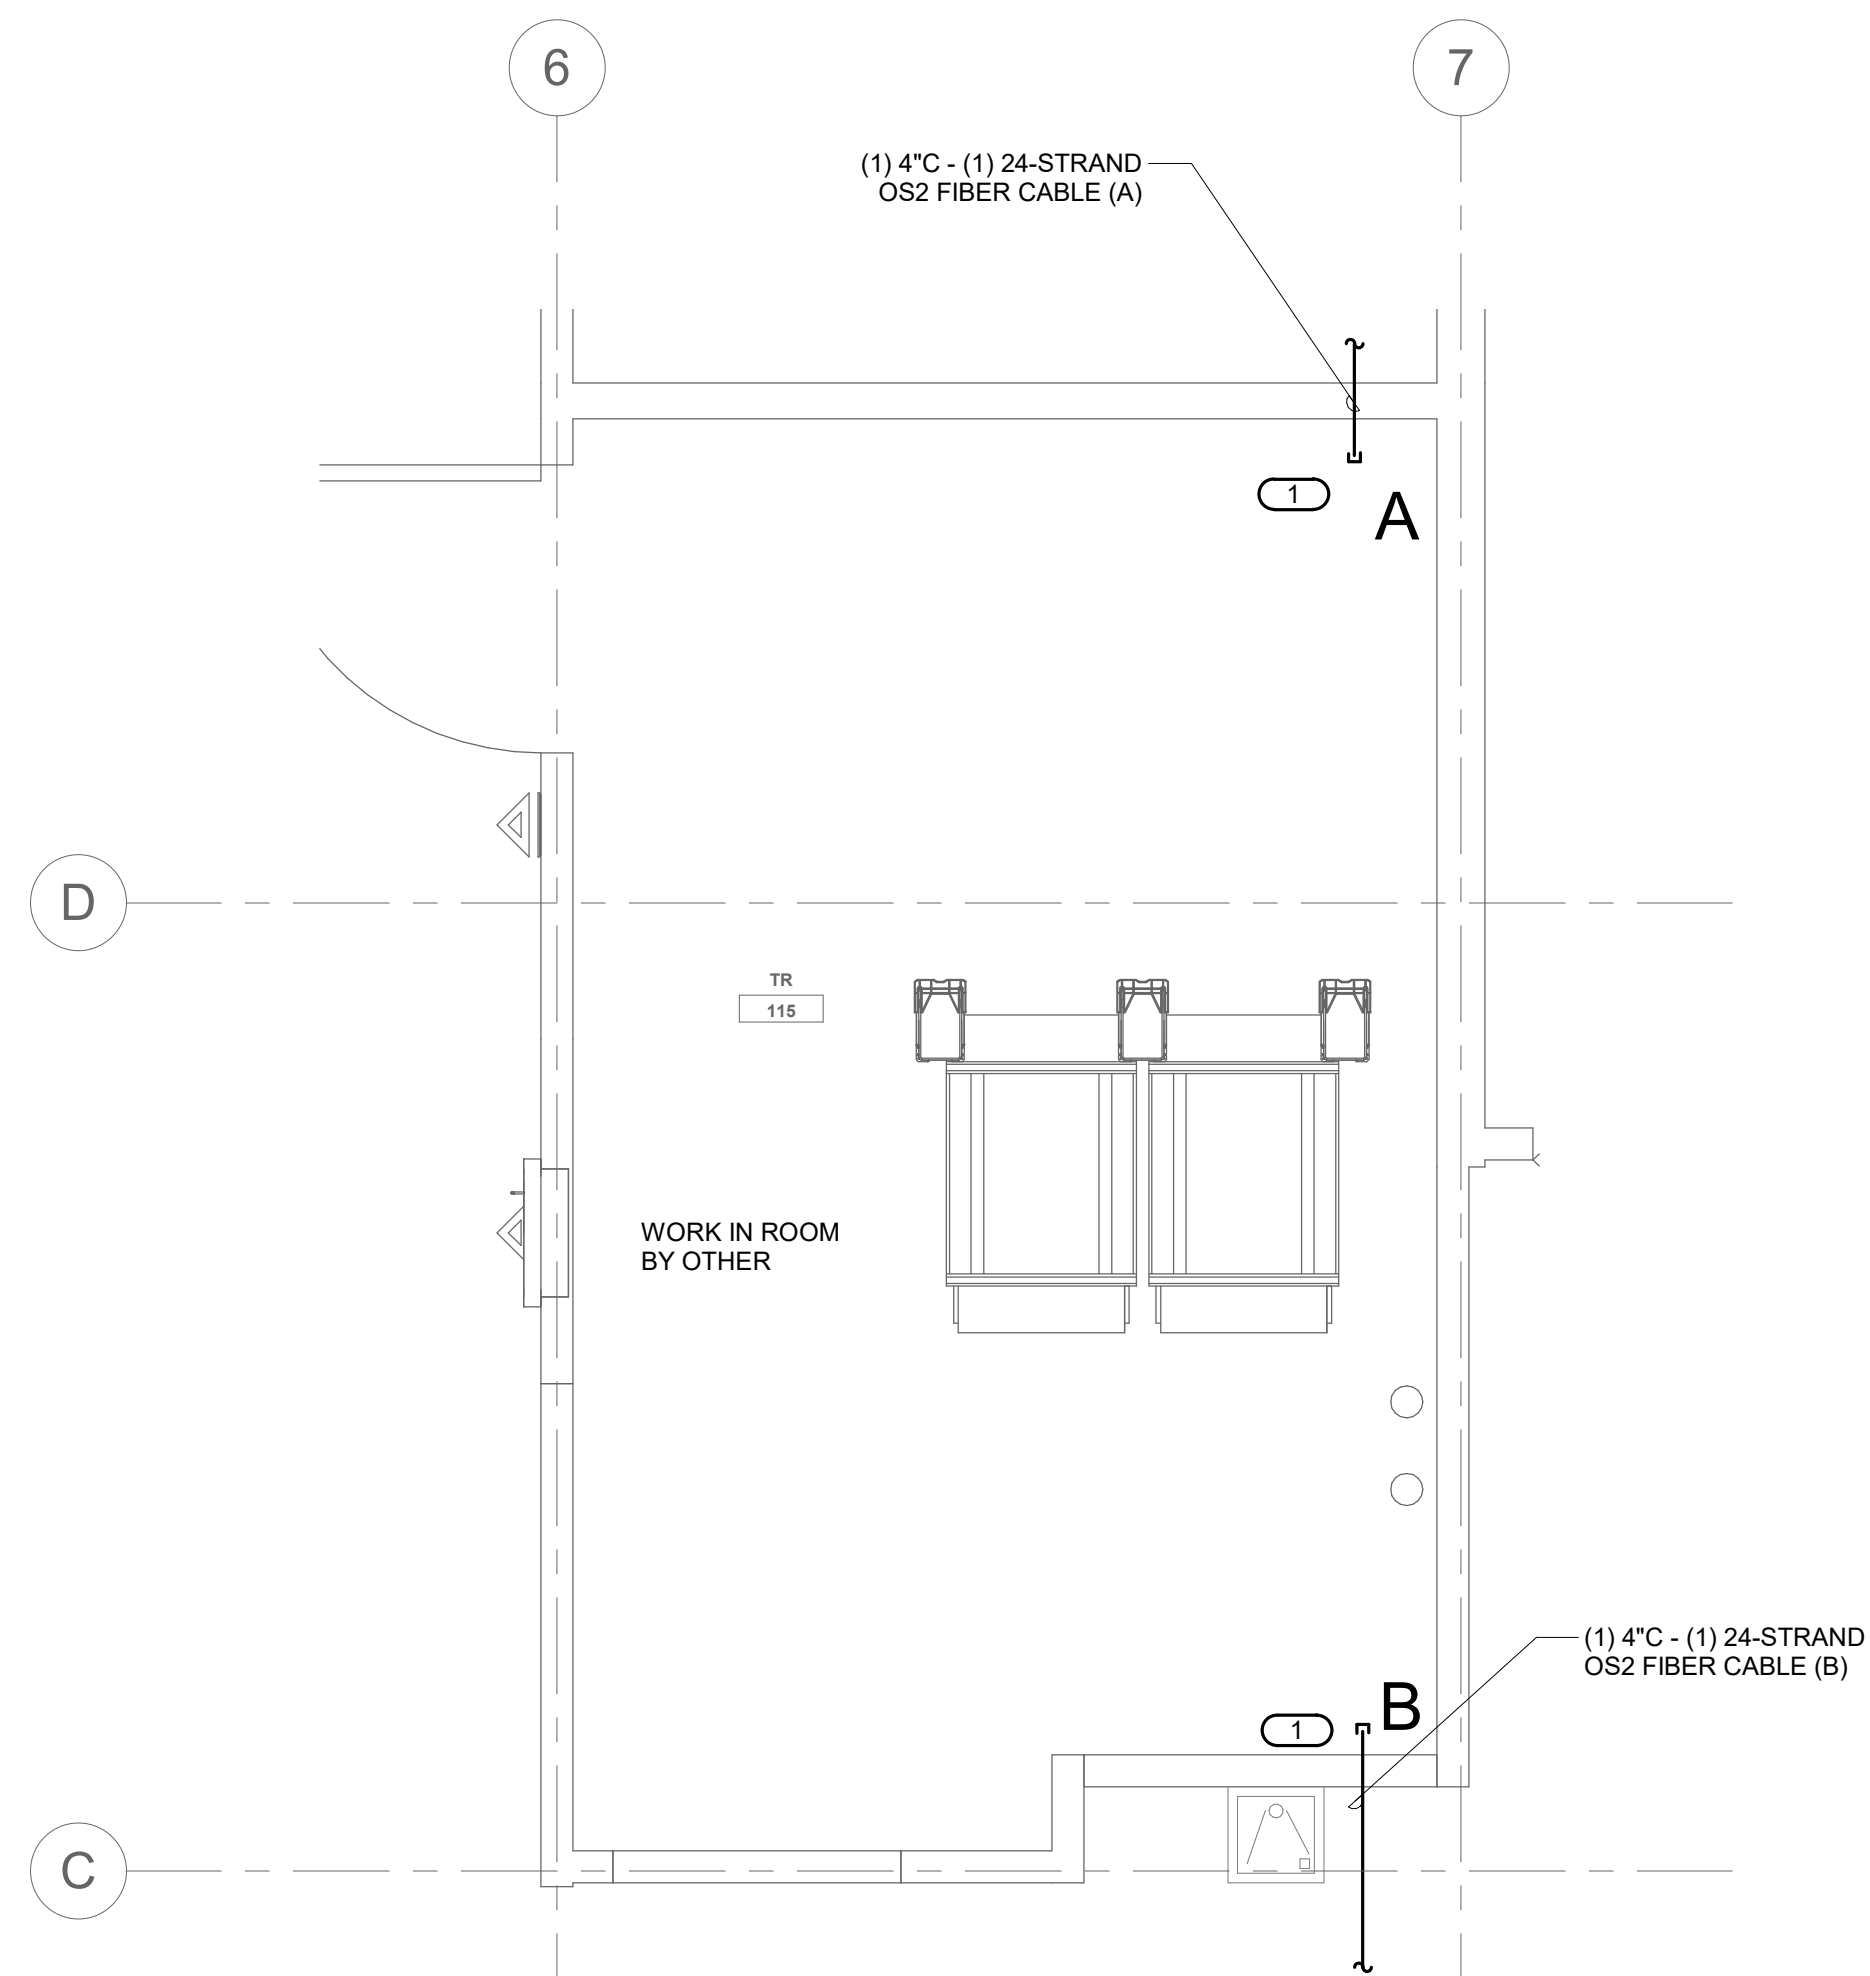


1 TELECOM ROOM ENLARGEMENT TR #115
1/2" = 1'-0"
NOTES:
1. REFER TO ELECTRICAL DRAWINGS FOR ROOM LAYOUT AND RACK ELEVATIONS.
2. ROUTE OPTICAL FIBER CABLE TO OVERHEAD CABLE TRAY AND TERMINATE IN FIBER DISTRIBUTION CABINET.
KEYNOTES: #
1. THROUGH WALL PENETRATION FOR BACKBONE CONDUIT. OPTICAL FIBER CABLE CONTINUES ON CABLE TRAY TO RACKS.

GROUP
THERAPY
ROOM
115

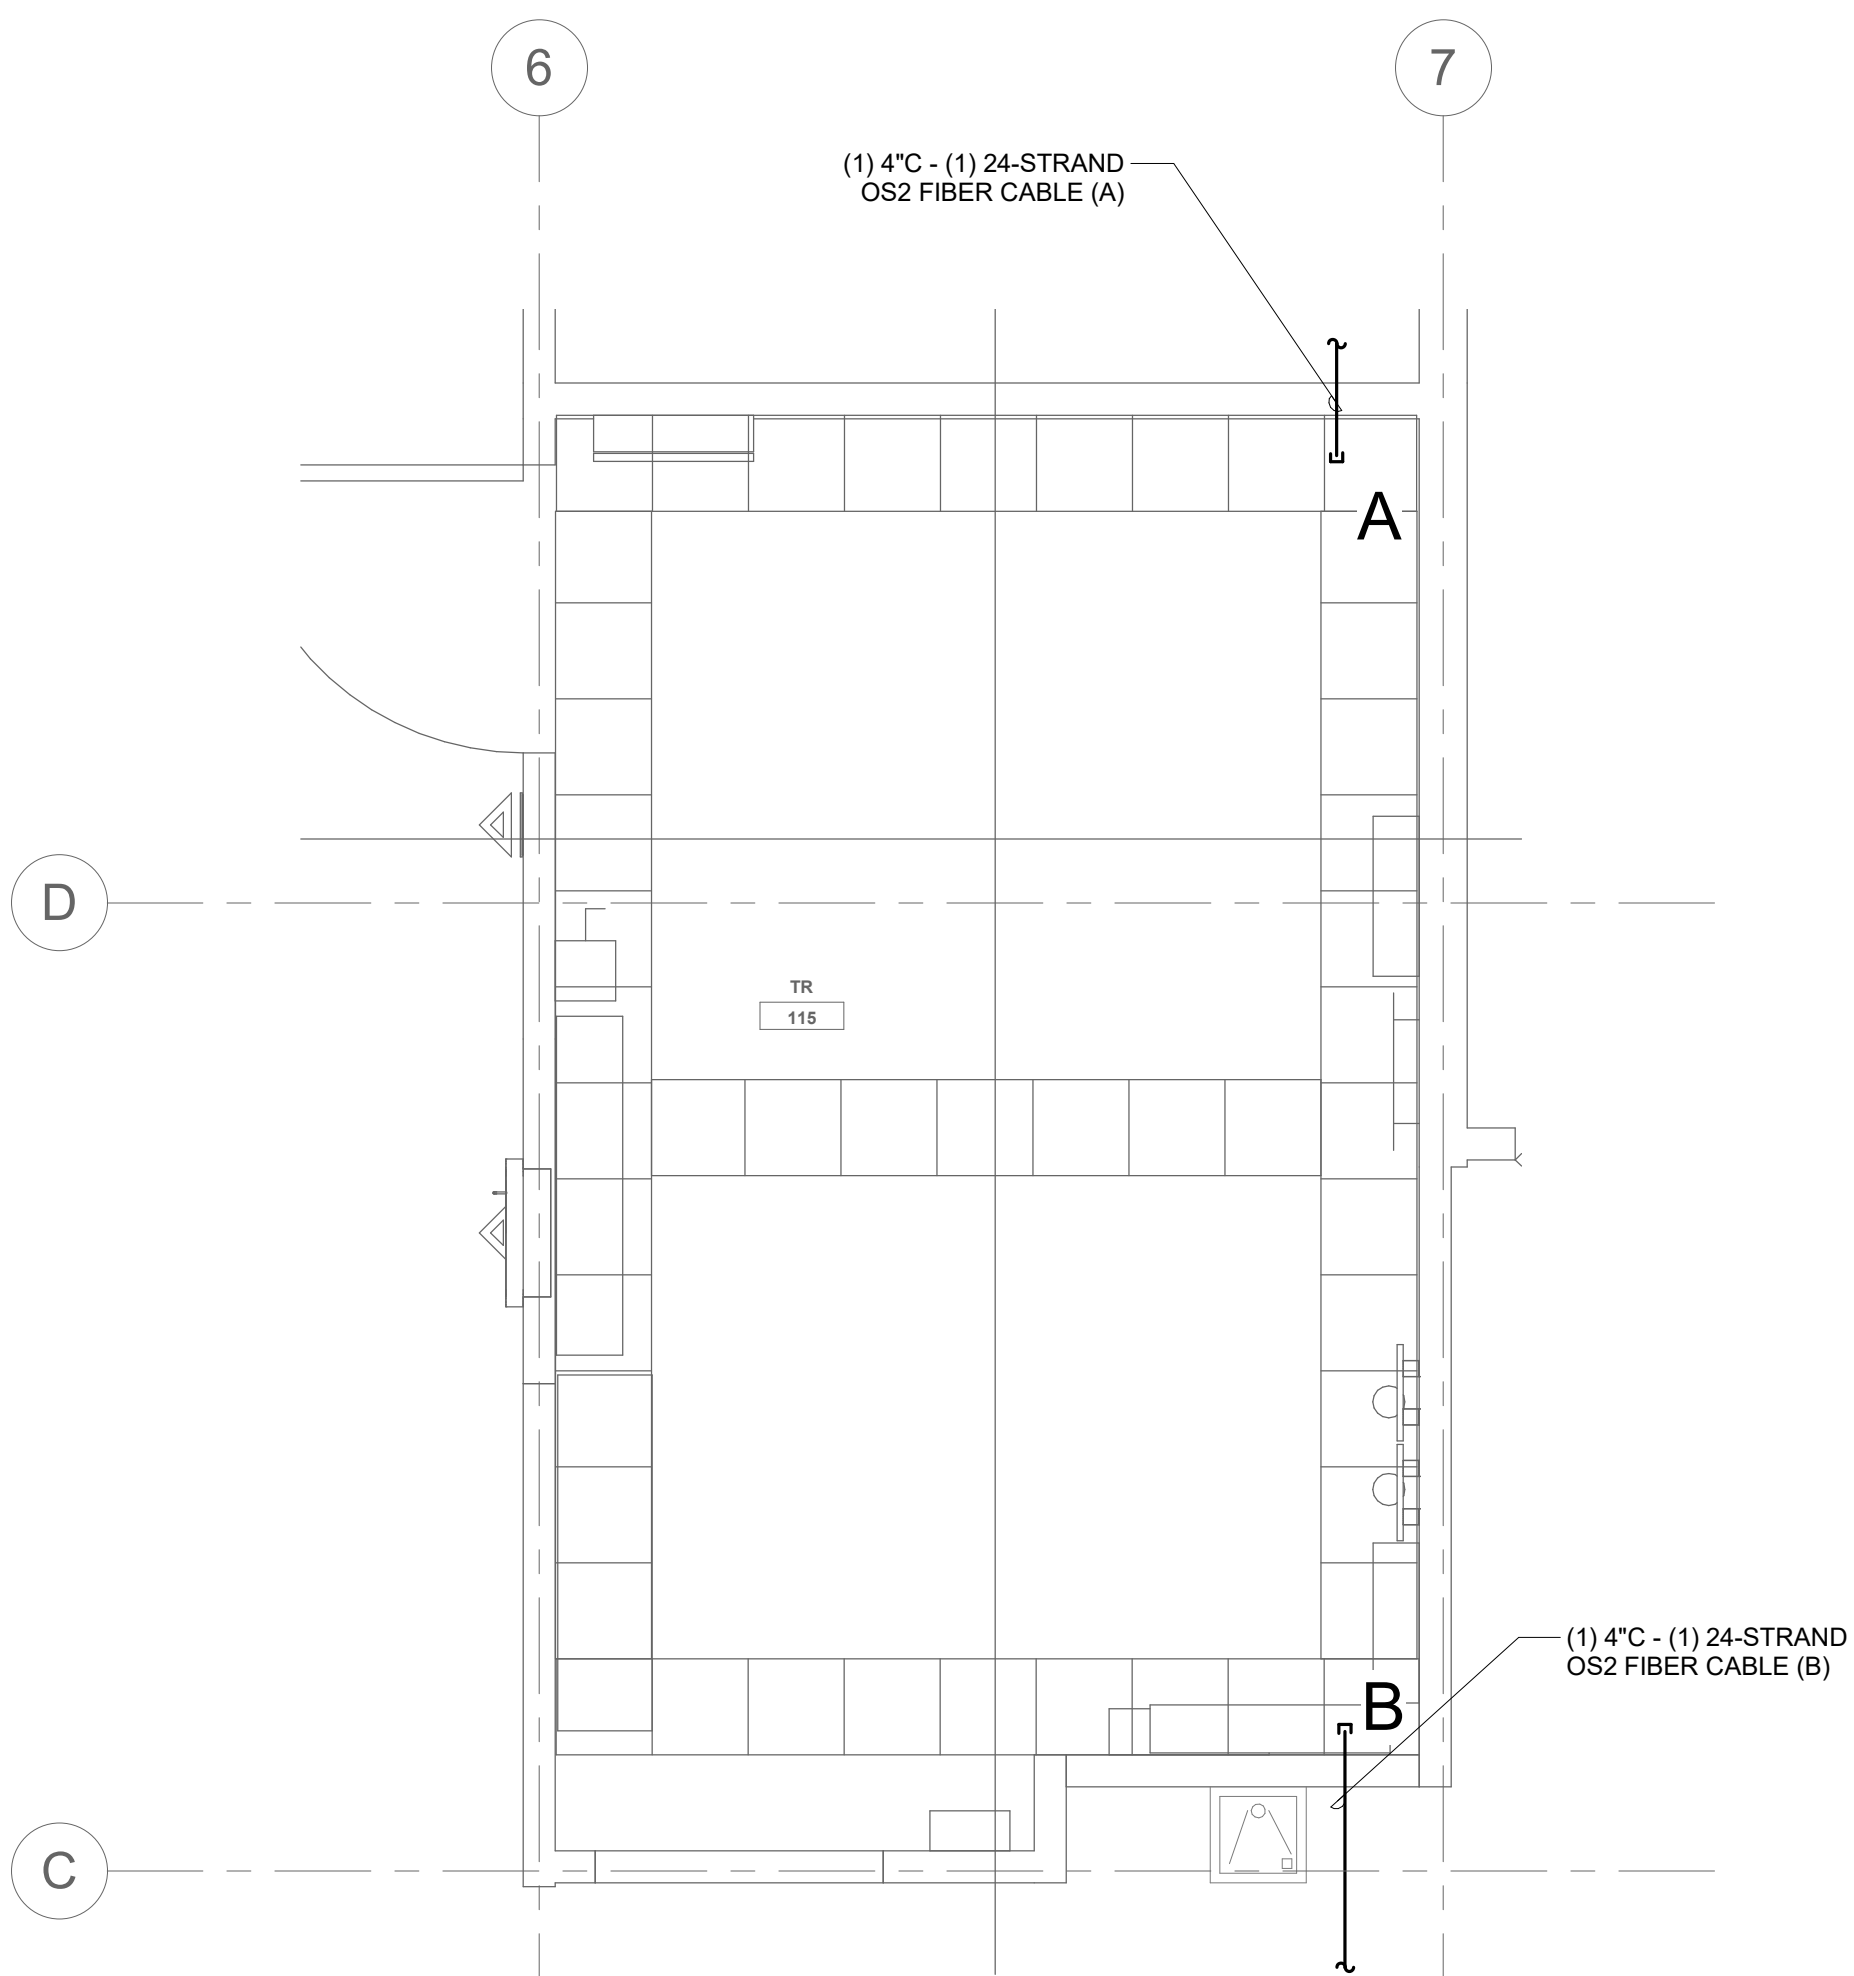

2 TELECOM ROOM PATHWAY TR #115
1/2" = 1'-0"


LEVEL 01

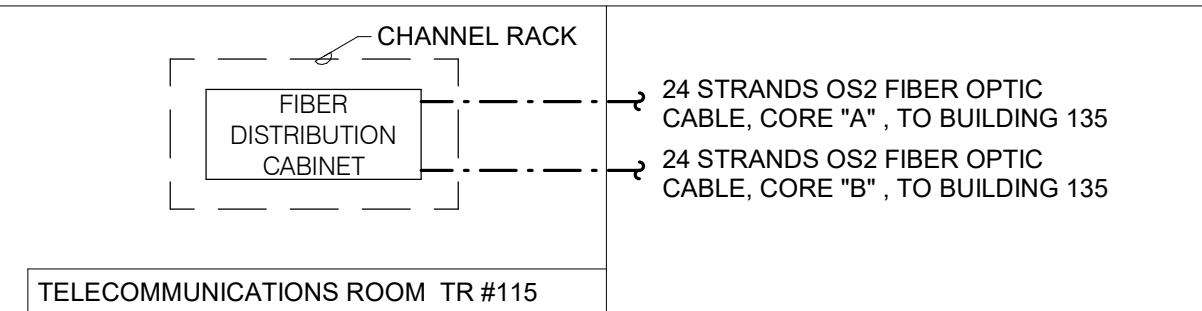

3 FIBER RISER DIAGRAM
NO SCALE
NOTES:
1. THIS RISER IS DIAGRAMMATIC AND MAY NOT SHOW ACTUAL ROUTING OR QUANTITIES OF MATERIALS SHOWN. THIS RISER IS SHOWN FOR CLARIFICATION OF CONNECTION(S), LOCATIONS AND CABLE TYPE. ALL INFORMATION OUTLETS ARE TYPICAL OF THE OUTLETS IN THE AREA SHOWN. REFER TO FLOOR PLANS FOR MORE SPECIFIC ROUTING INFORMATION. REFER TO SPECIFICATIONS FOR ADDITIONAL REQUIREMENTS.
2. REFER TO ELECTRICAL DRAWINGS FOR CHANNEL RACK AND FIBER OPTIC DISTRIBUTION CABINET SPECIFICATIONS

		CONSULTANT ENGINEERING DISCIPLINE:  www.imegcorp.com 225 W WASHINGTON STREET SUITE 2700 CHICAGO, IL 60606 P: 312.294.0501 F: 312.294.0003 PROJECT #22010109.00	ARCHITECT/ENGINEER OF RECORD A/E: SPEES DESIGN BUILD 23830 PACIFIC HIGHWAY S. SUITE 203 KENT, WA 98032  SPEESDESIGNBUILD	STAMP  REGISTERED COMMUNICATIONS DISTRIBUTION DESIGNER Bicsi Eddie C. Wilks, Jr. Reg. No. 1519026 EXPIRES 12-31-2025 RCDD <i>[Signature]</i>	Office of Construction and Facilities Management VA U.S. Department of Veterans Affairs	Drawing Title	Phase	Project Title	Project Number
						BLDG.148T TECHNOLOGY ENLARGED PLANS	100% CONSTRUCTION DOCUMENTS	EHRM INFRASTRUCTURE UPGRADES - HAMPTON	509-22-700
						Approved:	FULLY SPRINKLERED	Location	Building Number
								HAMPTON VA MEDICAL CENTER, HAMPTON, VIRGINIA	148T
								Issue Date	Checked
		05/09/2025	EW	IMEG	148TT-400 705 of 713				
Revisions:		Date:							

- KEY NOTES: C #
1. PROVIDE PENETRATIONS THRU WALL OF BLDG. 168 AND CONTINUE ROUTE OF CORE A CONDUITS ABOVE CEILING INTO PBX RM #10. ADJUST ROUTE THRU STORAGE ROOM AND MECH ROOM TO AVOID EXISTING DUCTWORK/PIPING.
 2. PROVIDE PULLBOX ON CONDUIT RUN TO EXTEND NEW CORE A BACKBONE FIBER CABLE TO NEW TR #10B.
 3. ROUTE CONDUIT ABOVE CEILING OVER TO NEW TR #10B. PROVIDE PENETRATION THRU WALL AND STUB CONDUIT INTO TR #10B.
 4. PROVIDE PENETRATION THRU WALL TO ROUTE CONDUITS FROM CRAWL SPACE IN BLDG #110 INTO CRAWL SPACE OF BLDG #168 AND BELOW BATTERY ROOM #10A.
 5. PROVIDE PENETRATION THRU FLOOR OF BATTERY ROOM AND ROUTE CONDUITS (STACKED) UP INTO BATTERY ROOM. CONTINUE ROUTE OF CONDUITS TO ABOVE CEILING AND INTO PBX #10 ROOM.
 6. PROVIDE PULLBOX ON CONDUIT RUN TO EXTEND NEW CORE B BACKBONE FIBER CABLE TO NEW TR #10B.
 7. PROVIDE PENETRATIONS THRU CMU WALL TO ROUTE BACKBONE CONDUITS BETWEEN BLDGS 135 AND 168 AS INDICATED. COORDINATE EXACT PENETRATION LOCATIONS WITH STRUCTURAL.

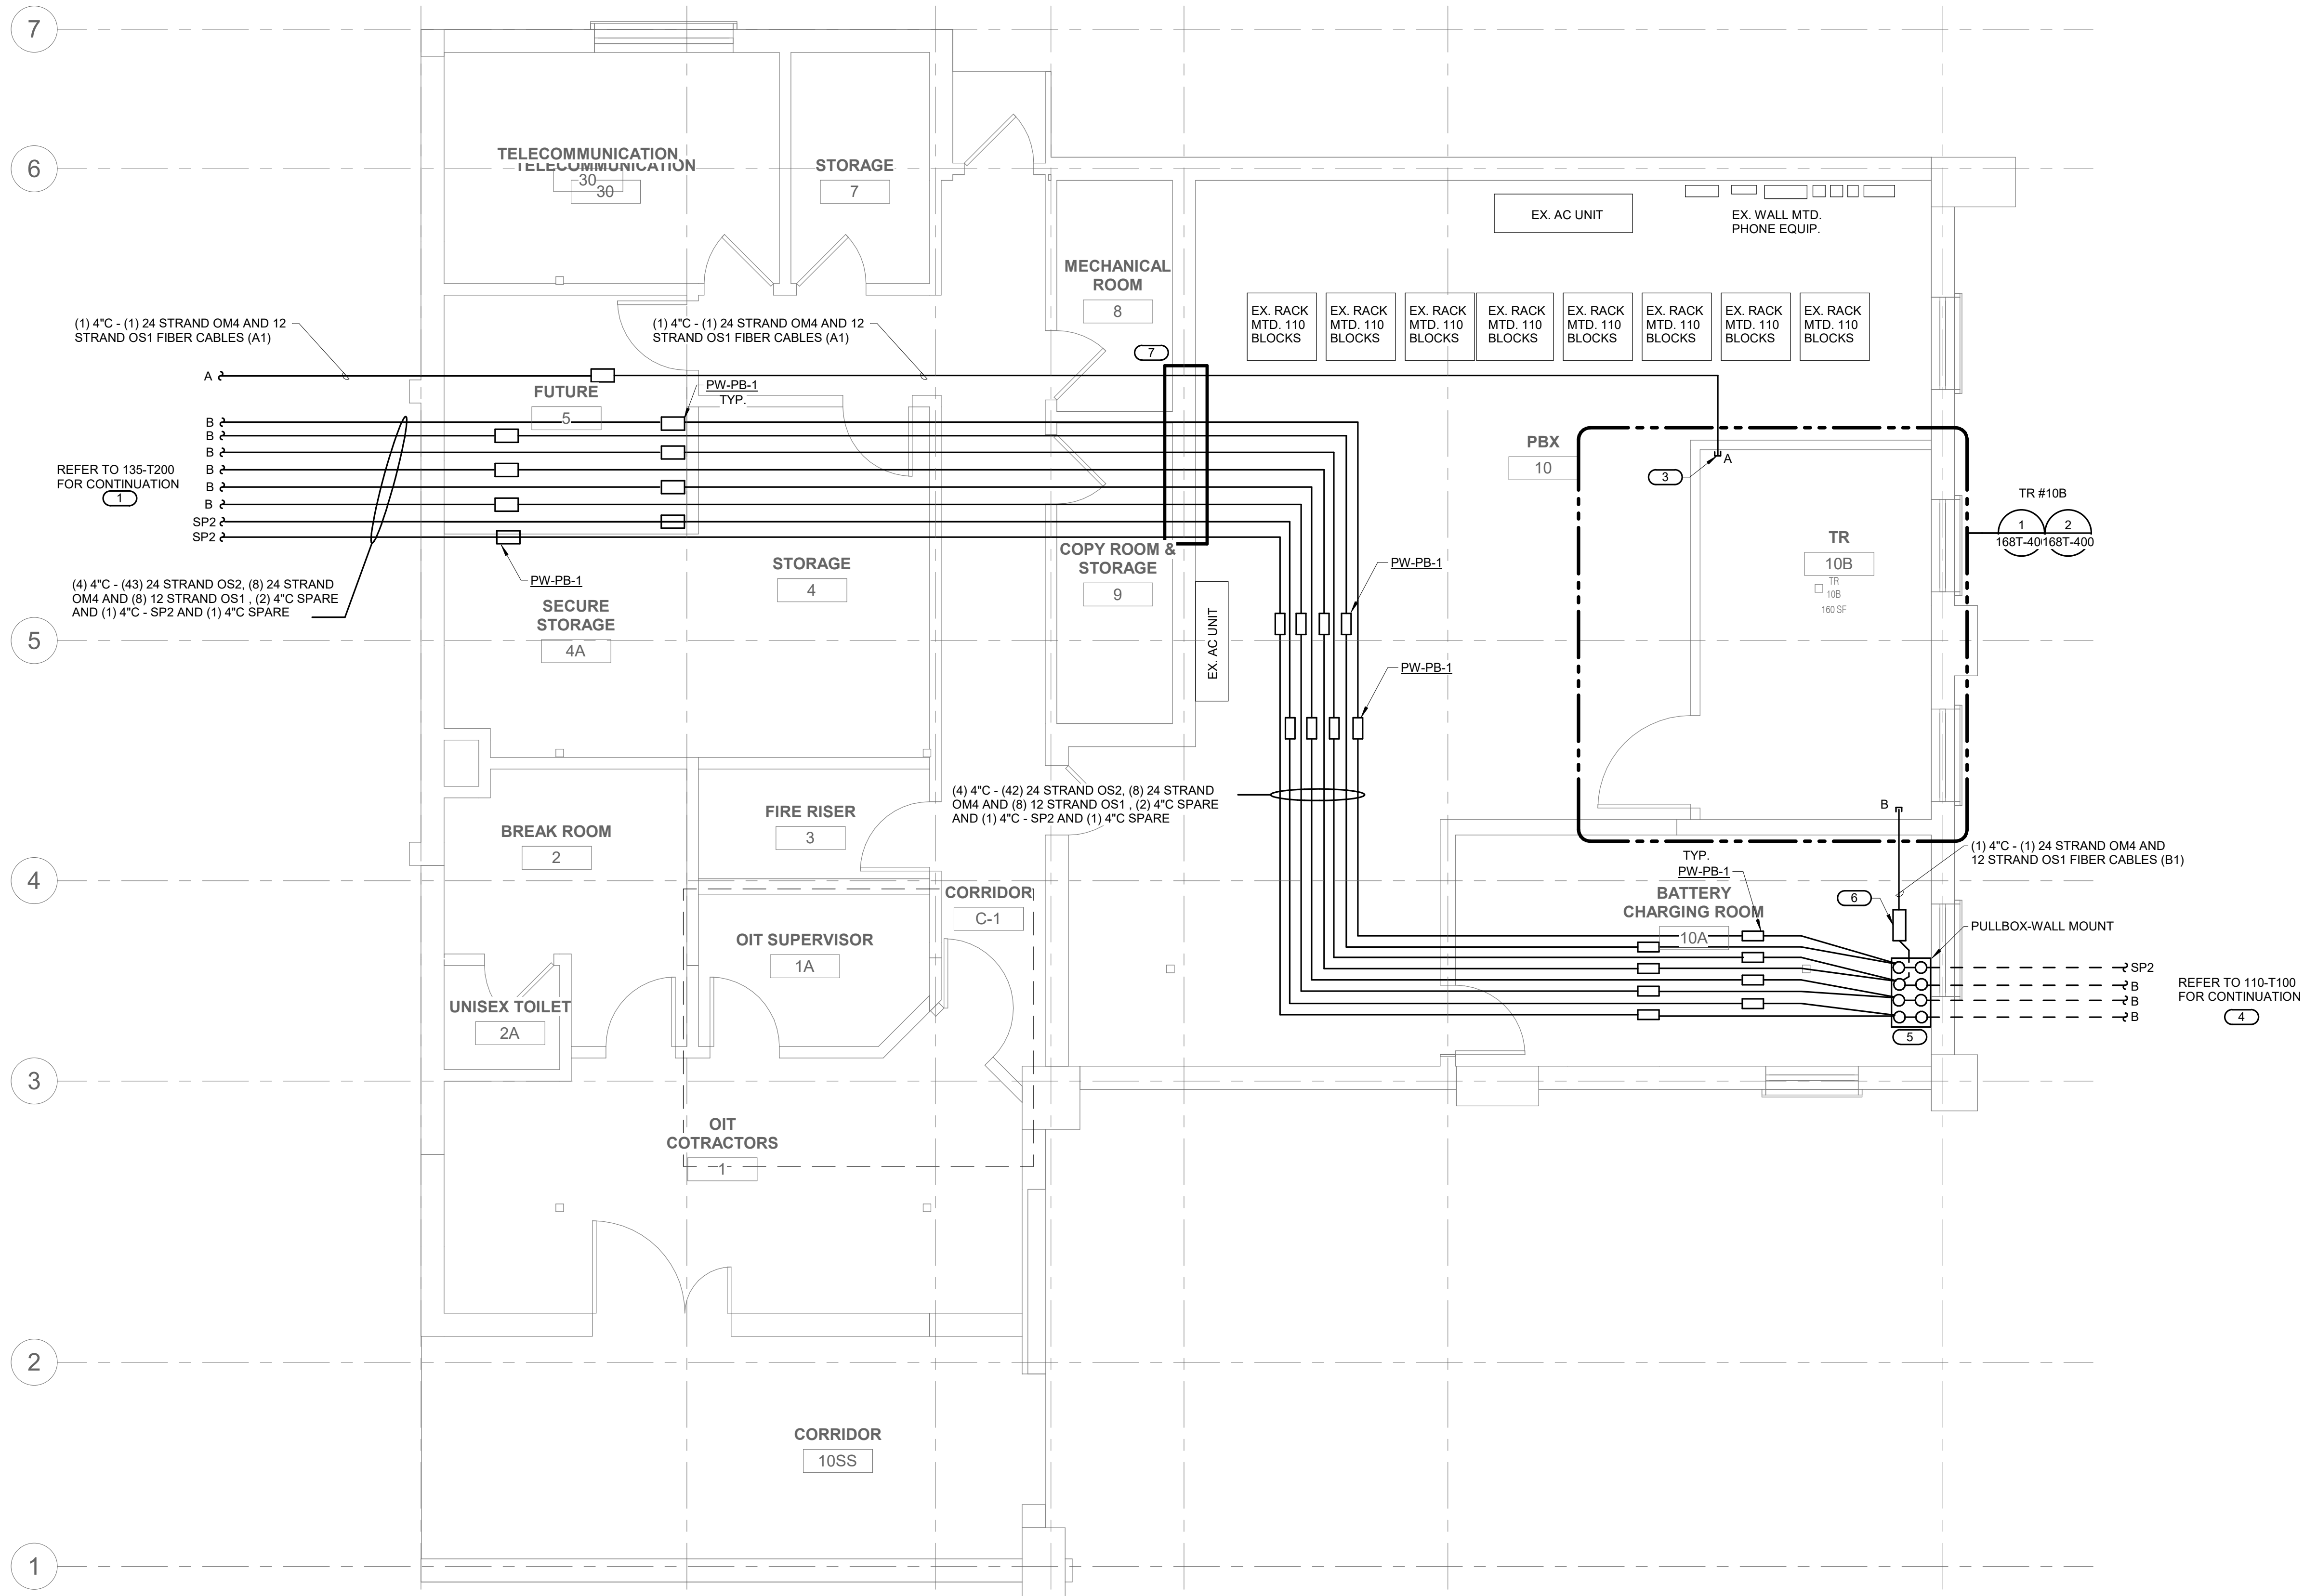

1 LEVEL 00 PLAN - TECHNOLOGY
1/4" = 1'-0"

Revisions:	CONSULTANT		ARCHITECT/ENGINEER OF RECORD		STAMP	Office of Construction and Facilities Management	Drawing Title BLDG. 168 LEVEL 00 PLAN - TECHNOLOGY	Phase 100% CONSTRUCTION DOCUMENTS	Project Title EHRM INFRASTRUCTURE UPGRADES - HAMPTON		Project Number 509-22-700					
	ENGINEERING DISCIPLINE:		A/E:						Building Number 168		Building Number 168					
	DATE:		SPEEDSDESIGNBUILD						Location HAMPTON VA MEDICAL CENTER, HAMPTON, VIRGINIA		Drawing Number 168T-100					
	DATE:		DATE:						DATE:		DATE:		DATE:		DATE:	
DATE:		DATE:		DATE:		DATE:		DATE:		DATE:		DATE:				
DATE:		DATE:		DATE:		DATE:		DATE:		DATE:		DATE:				
DATE:</																

A


B

C

D

E

F

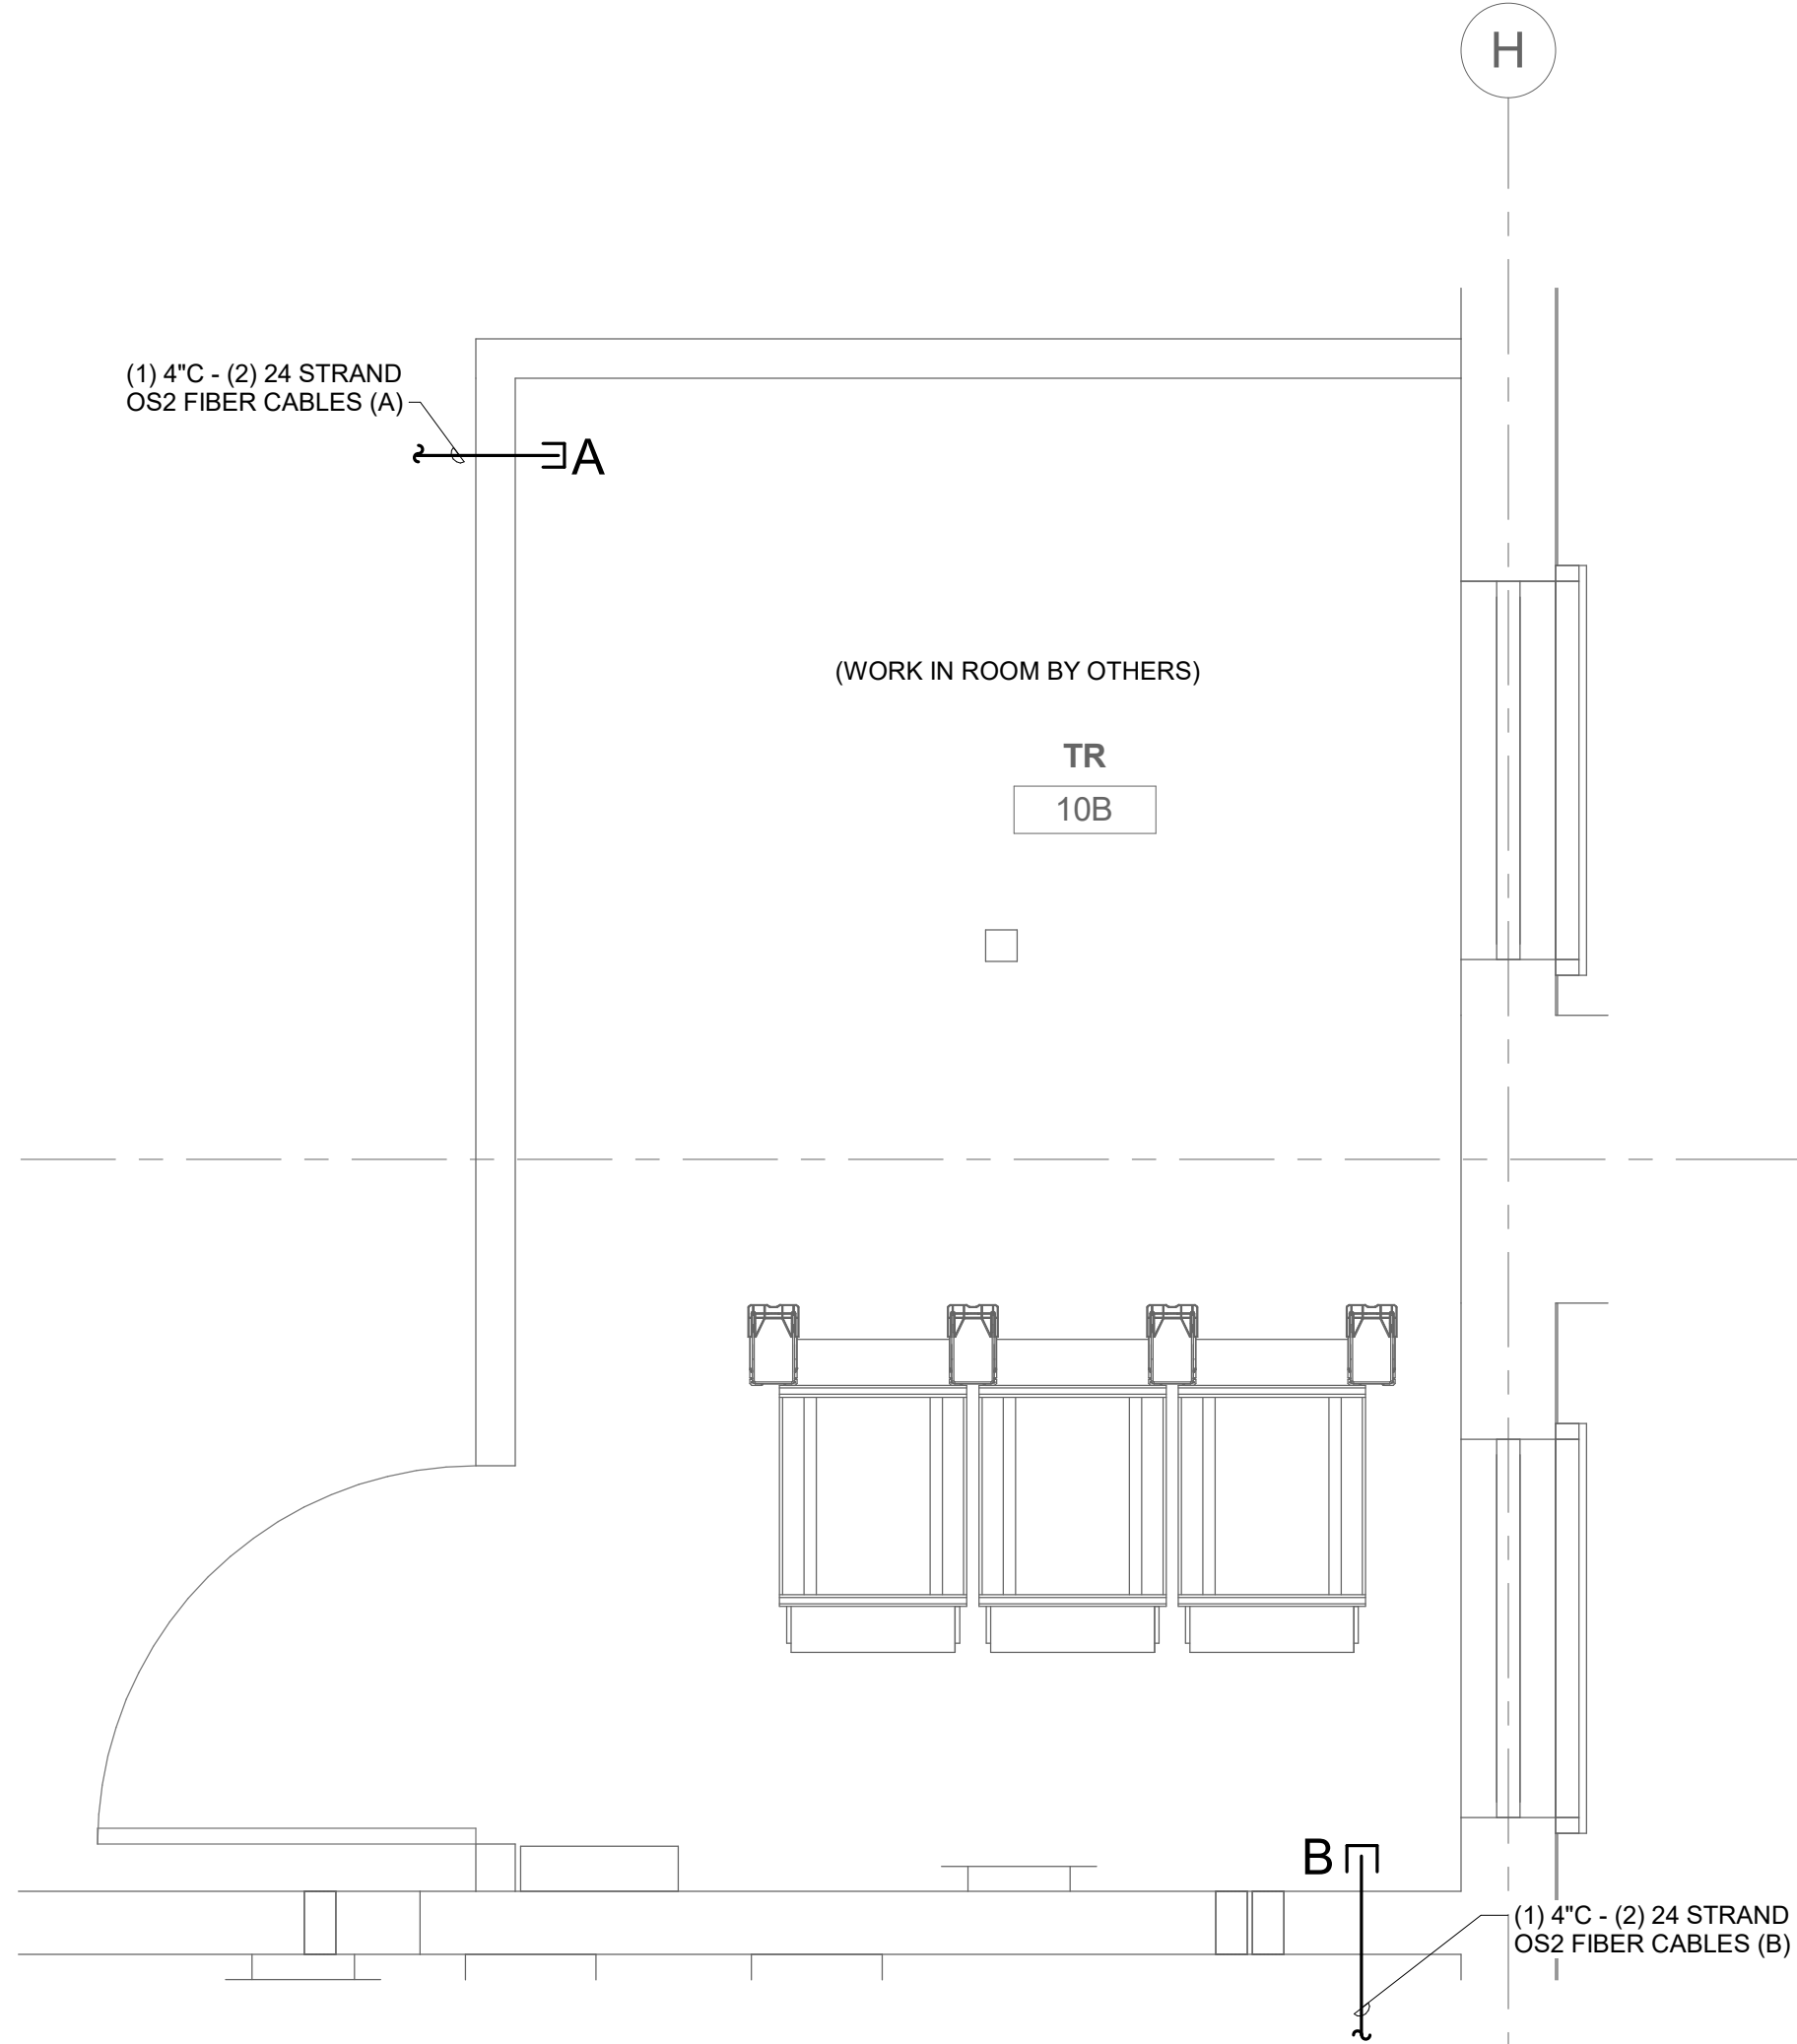

NORTH


1

1/2" = 1'-0"

TELECOM ROOM ENLARGEMENT TR #10B

KEY NOTES: C #

1. ROUTE CONDUITS UP TO CEILING HEIGHT AND STUB AND BUSH ABOVE CABLE TRAY. CONTINUE ROUTE OF CORE A OPTICAL FIBER CABLES ON CABLE TRAY, THRU PATHWAYS AND INTO MCR #25.

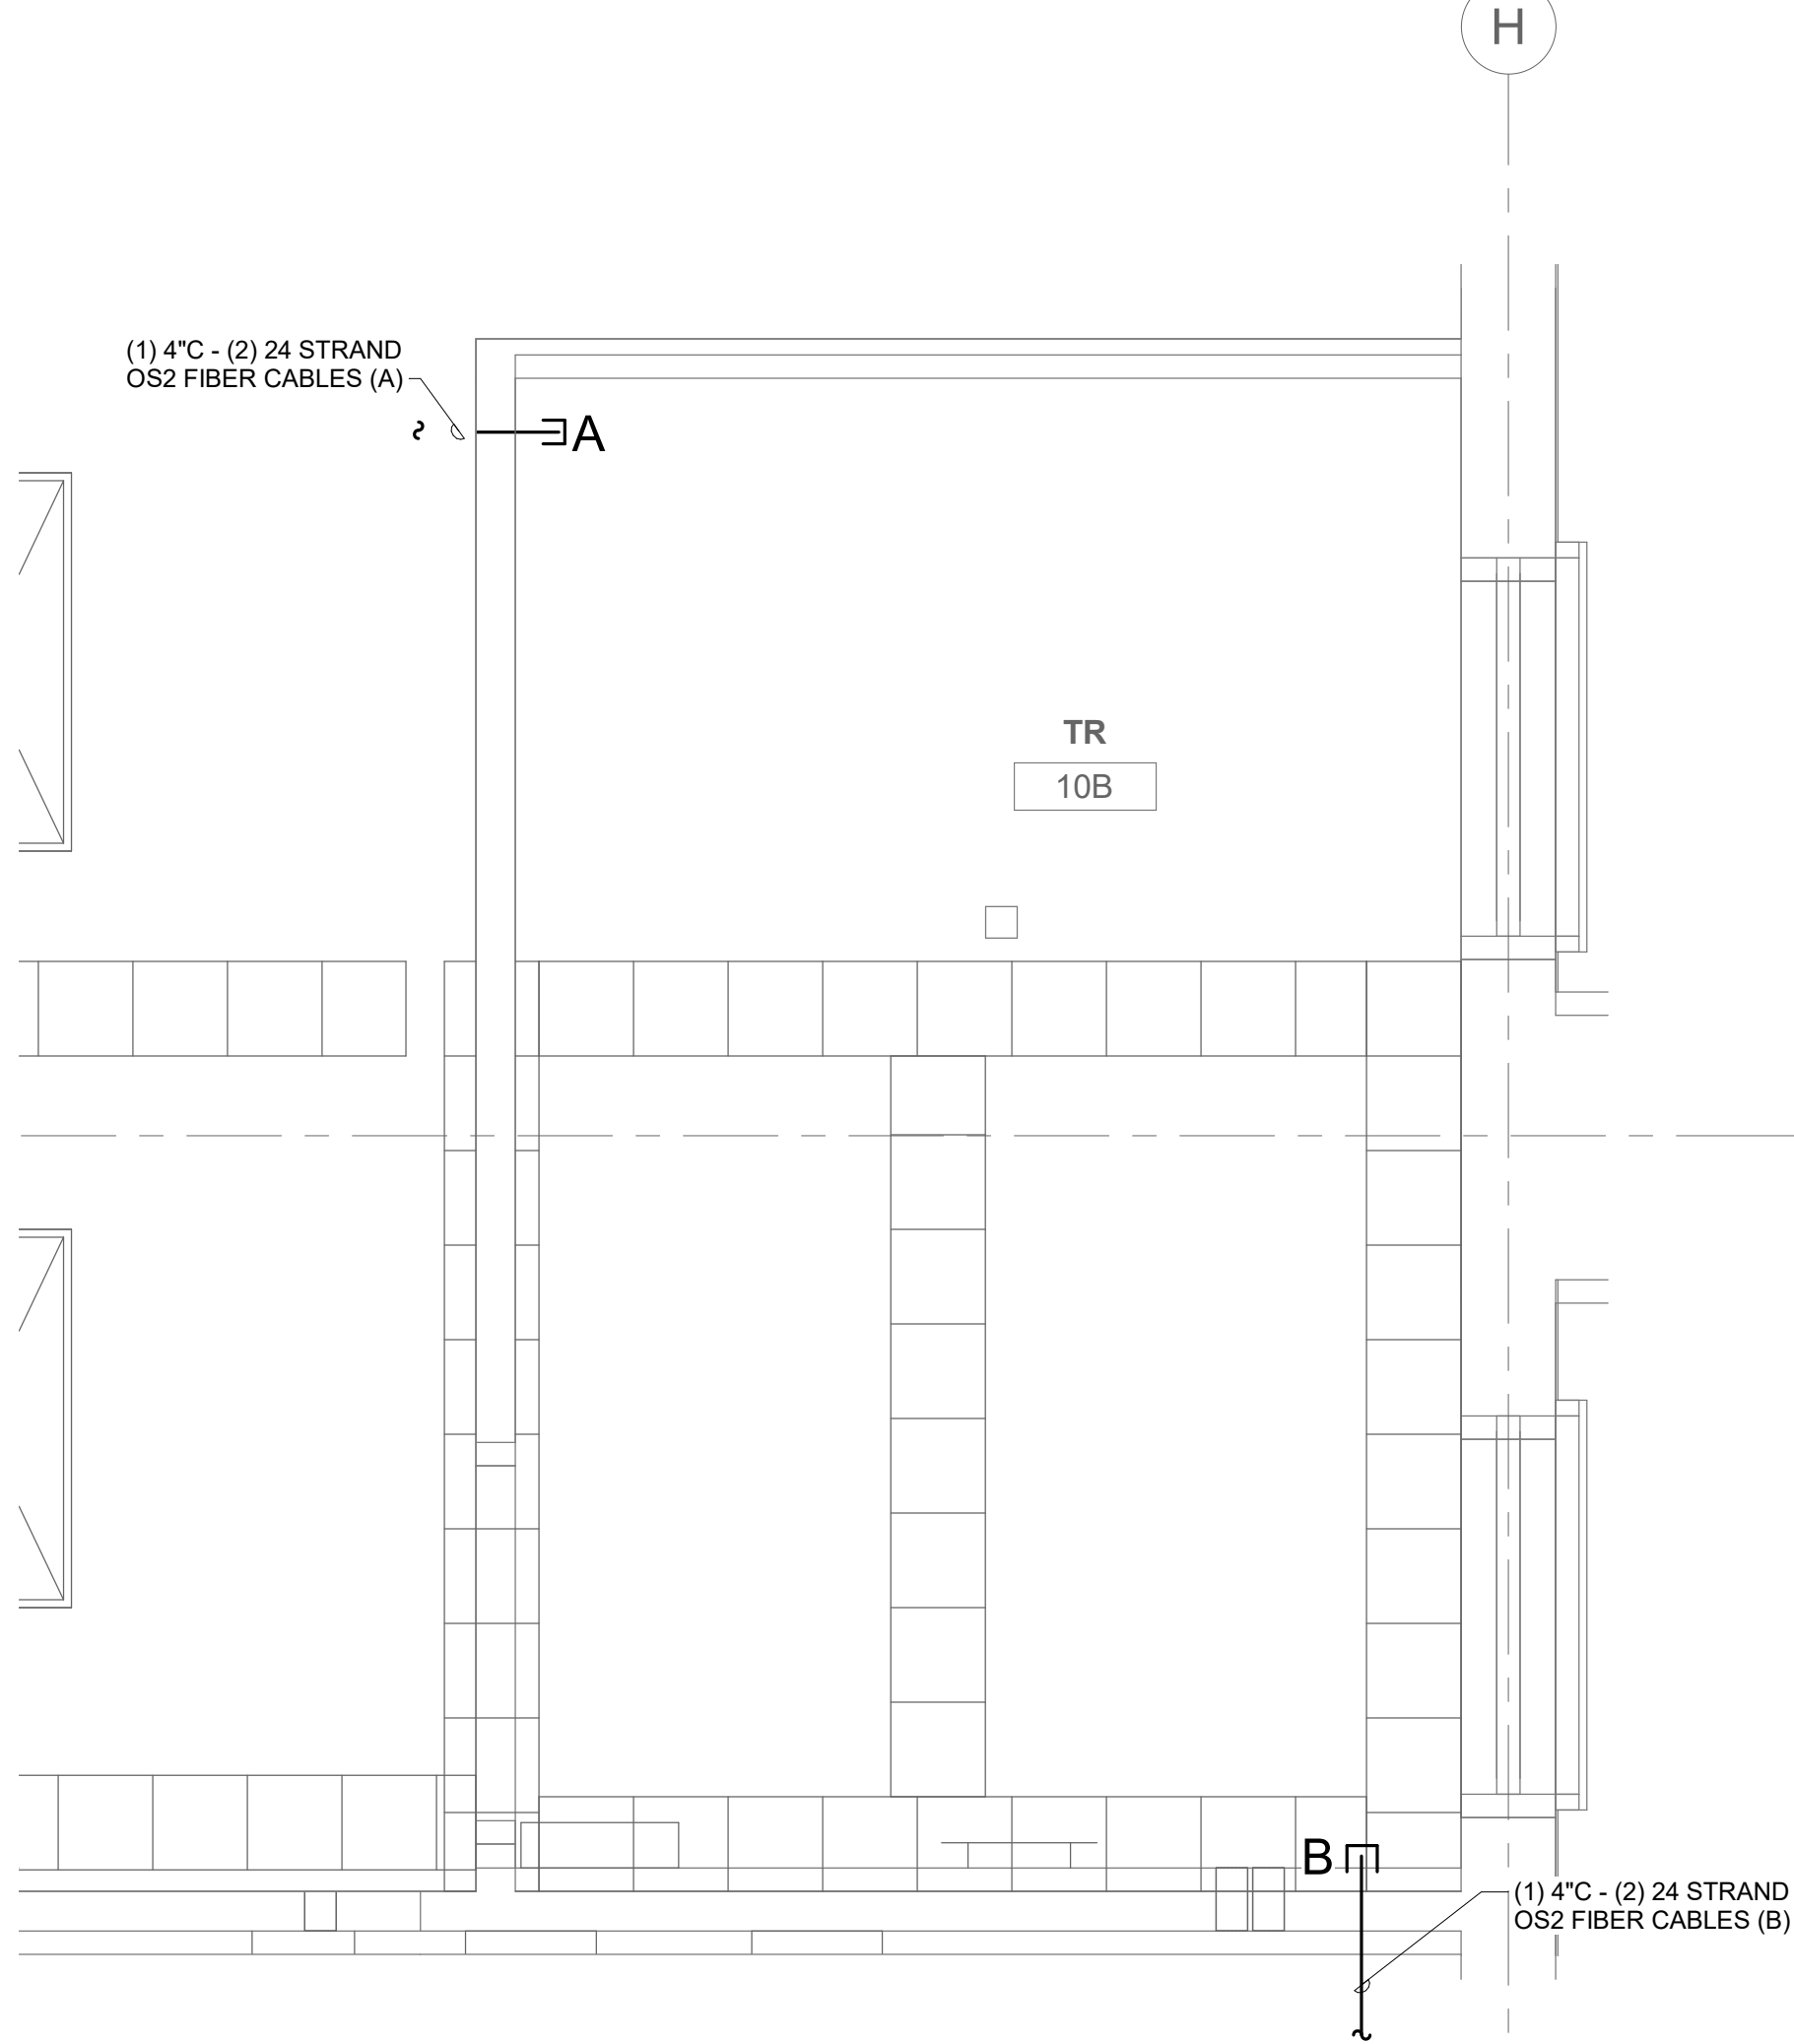


NORTH

2

1/2" = 1'-0"

TELECOM ROOM PATHWAY TR #10B

LEVEL 00

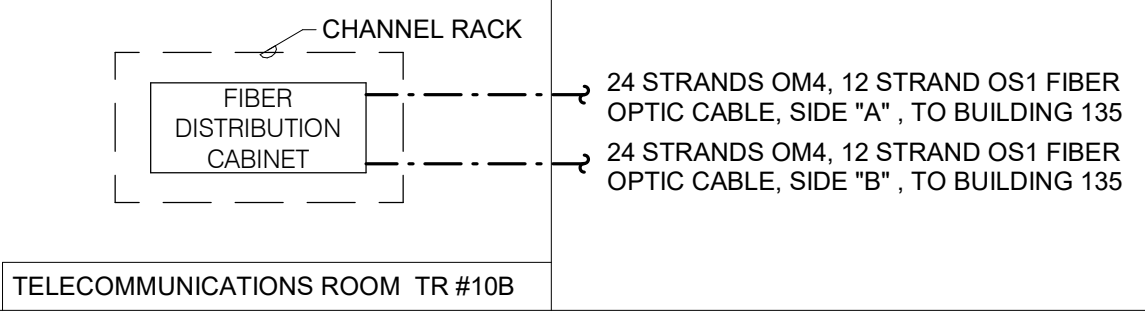

- 3

FIBER AND COPPER RISER DIAGRAM
- NO SCALE
- NOTES:
1. THIS RISER IS DIAGRAMMATIC AND MAY NOT SHOW ACTUAL ROUTING OR QUANTITIES OF MATERIALS SHOWN. THIS RISER IS SHOWN FOR CLARIFICATION OF CONNECTION(S), LOCATIONS AND CABLE TYPE. ALL INFORMATION OUTLETS ARE TYPICAL OF THE OUTLETS IN THE AREA SHOWN. REFER TO FLOOR PLANS FOR MORE SPECIFIC ROUTING INFORMATION. REFER TO SPECIFICATIONS FOR ADDITIONAL REQUIREMENTS.
2. REFER TO ELECTRICAL DRAWINGS FOR CHANNEL RACK AND FIBER OPTIC DISTRIBUTION CABINET SPECIFICATIONS

A

B

C


D

E

F

- SHEET NOTES:**
1. REFER TO SITEPLAN TS001 FOR ADDITIONAL INFORMATION.
 2. REFER TO TS00 AND 00-TS01 FOR CAMPUS OPTICAL FIBER RISER DIAGRAMS.
 3. REFER TO 2/T400 FOR HANDHOLE DETAIL.
 4. REFER TO ENLARGED PLANS FOR ADDITIONAL INFORMATION.
 5. ROUTES SHOWN THRU CRAWL SPACES ARE "SUGGESTED" ROUTES. FIELD VERIFY EXACT ROUTES.
 6. SEAL ALL PENETRATIONS TO MAINTAIN FIRE-RATINGS OF WALL, CEILING AND FLOORS.


- KEY NOTES: (C #)**
1. PROVIDE PULLBOX ON EXTERIOR WALL AT HEIGHT ABOVE CEILING. ROUTE CONDUITS UP WALL INTO PULLBOX. PROVIDE PENETRATION THRU WALL AND ROUTE CONDUITS AT GROUND FLOOR CEILING HEIGHT, THRU CORRIDOR, INTO TR #161.

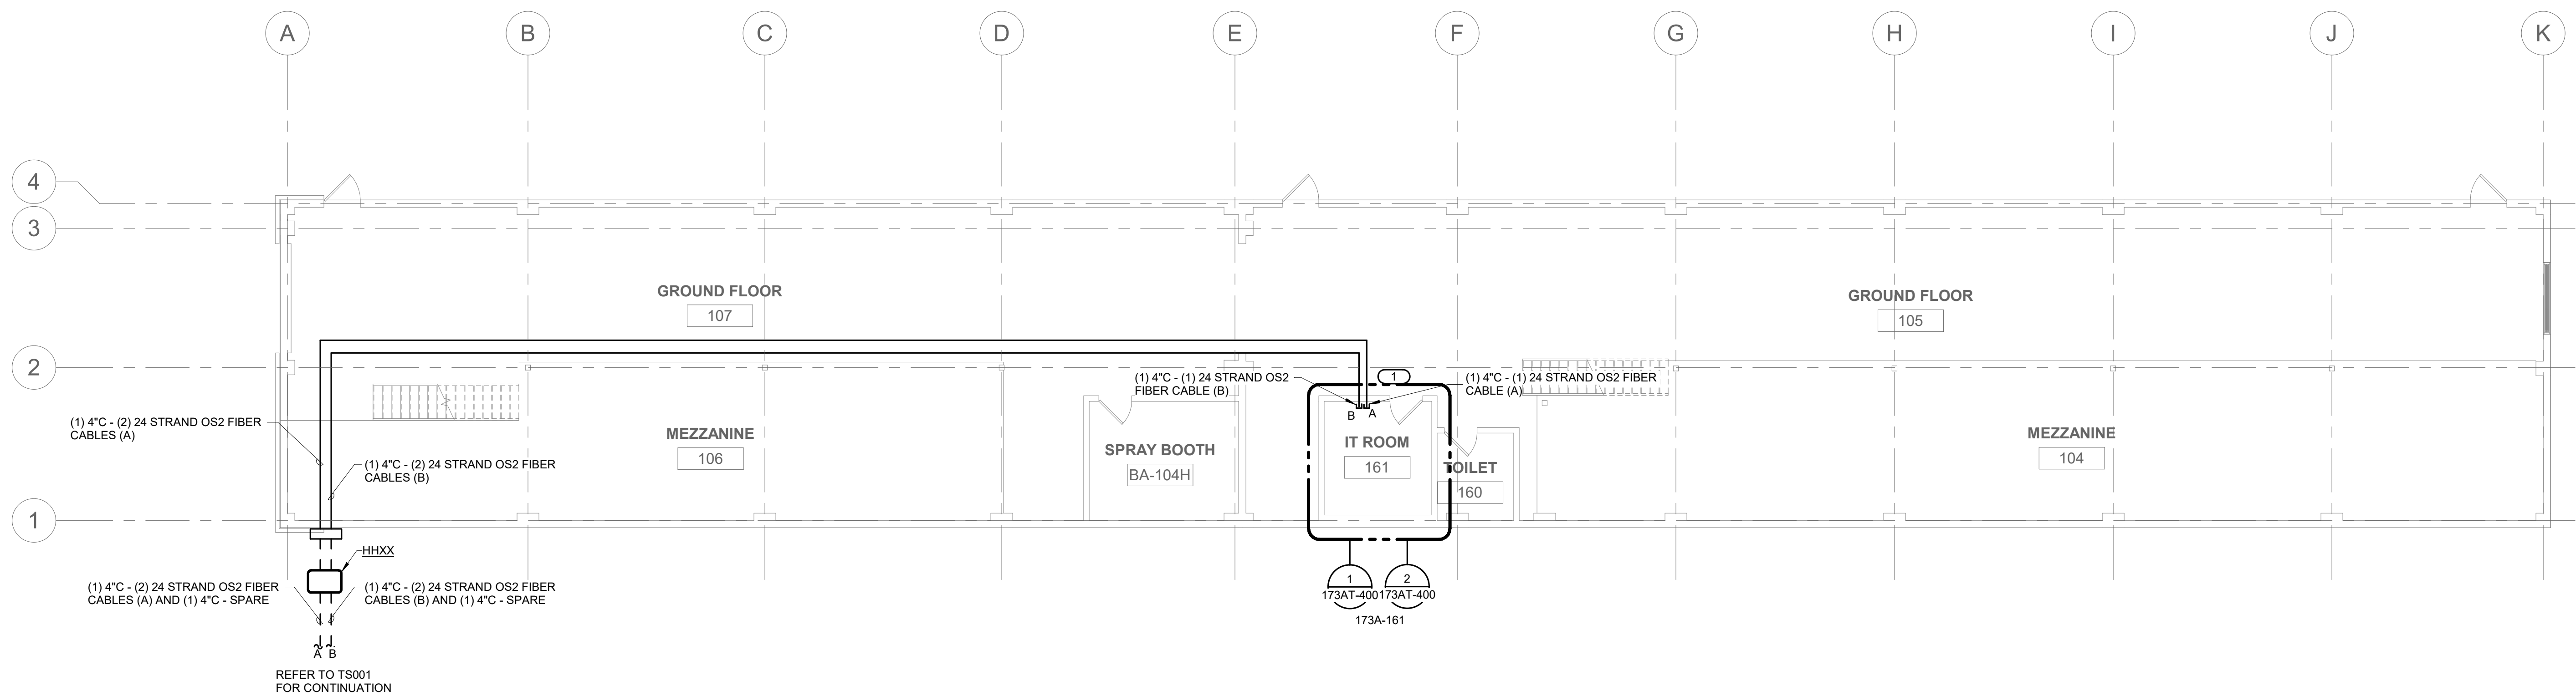

1 LEVEL 01 PLAN - TECHNOLOGY
1/8" = 1'-0"

--	--	

BM 360/509-22-700
VA Hampton
E:\161505-700.B173A_T_021.rvt
8/13/2025 12:57:28 PM

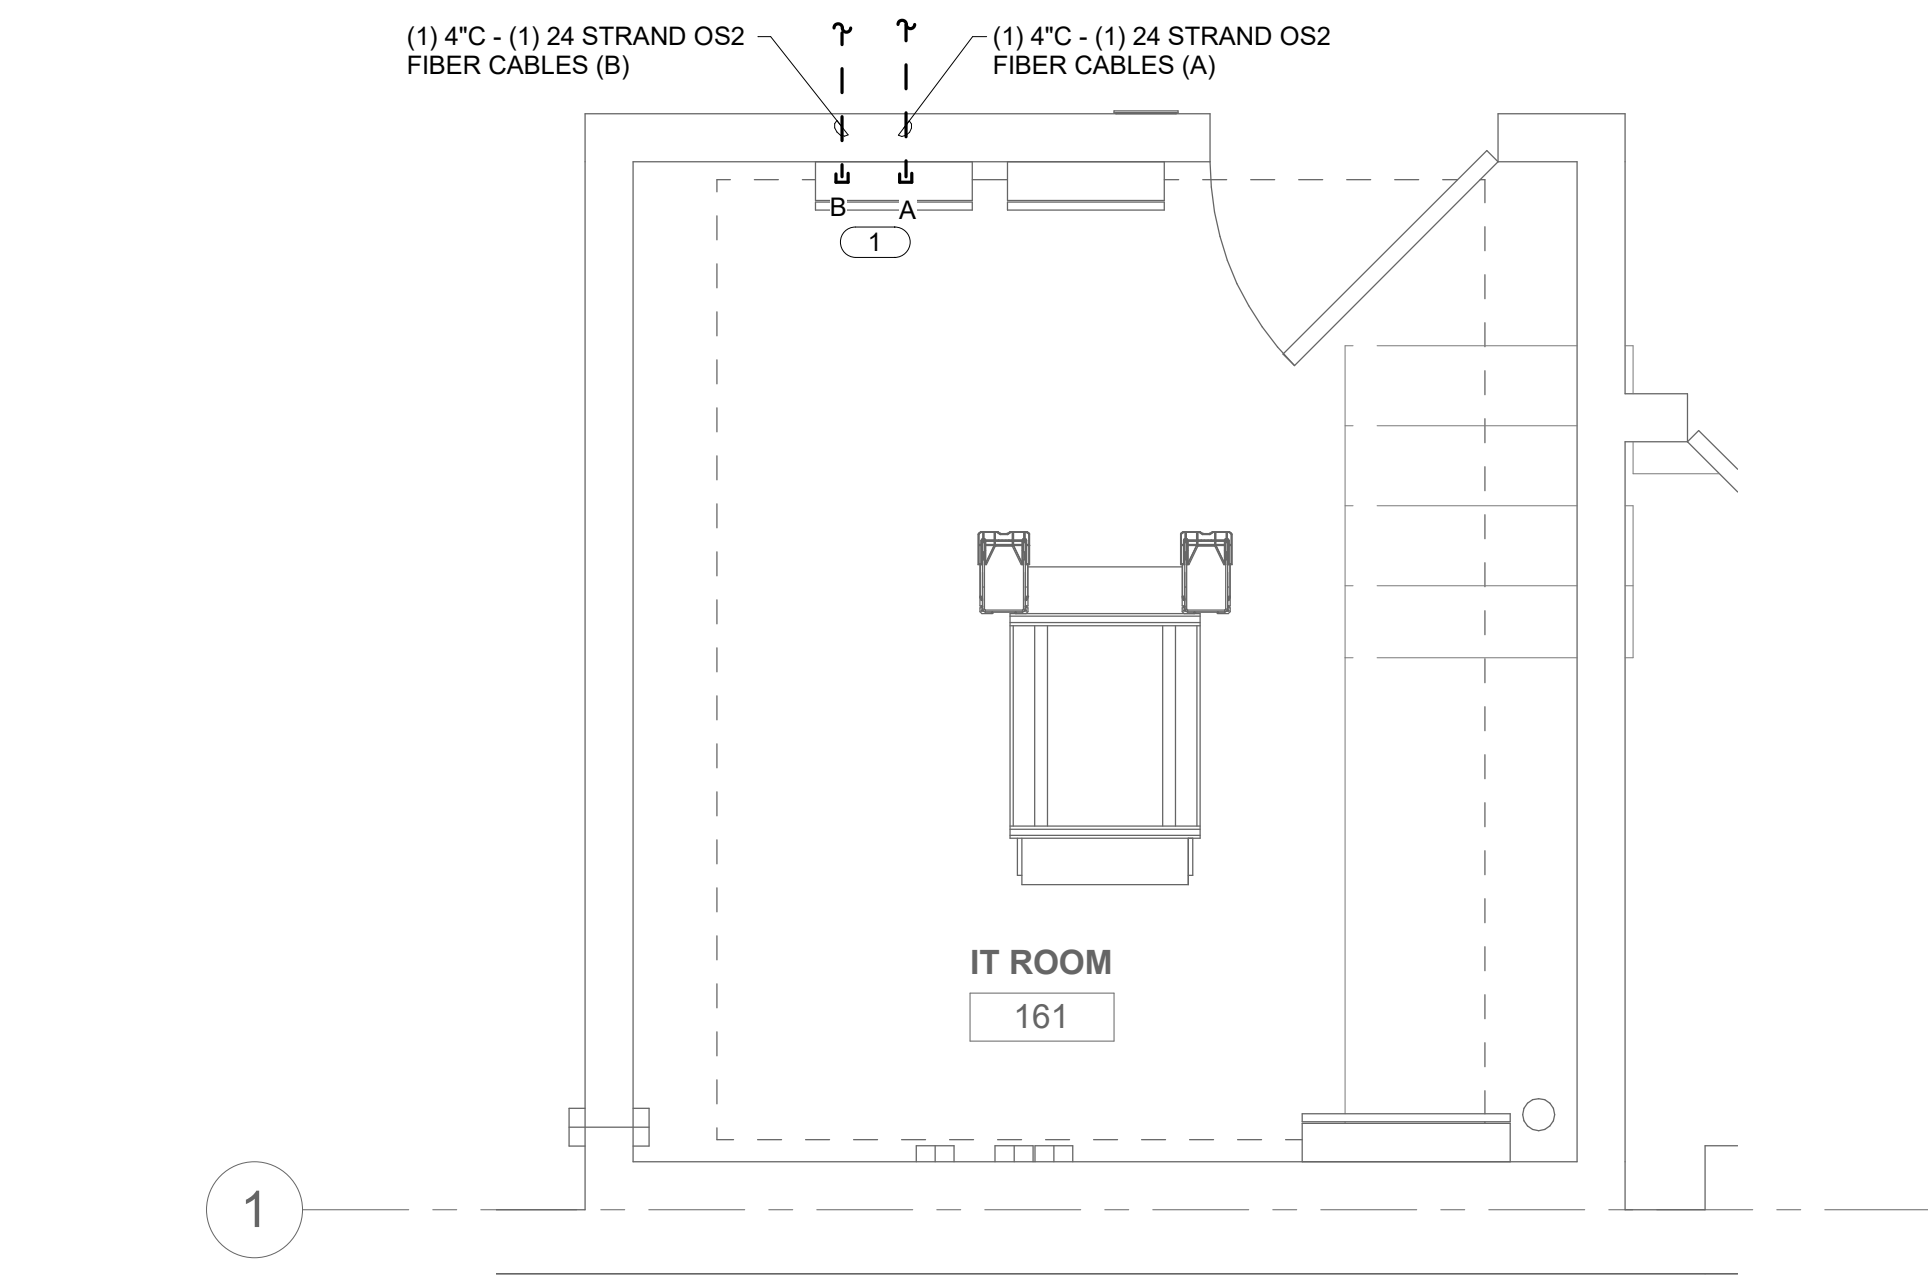

1

1/2" = 1'-0"

TELECOM ROOM ENLARGEMENT PLAN - TR-173A-161

NOTES:


1. REFER TO ELECTRICAL DRAWINGS FOR ROOM LAYOUT AND RACK ELEVATIONS.

2. ROUTE OPTICAL FIBER CABLE TO OVERHEAD CABLE TRAY AND TERMINATE IN FIBER DISTRIBUTION CABINET.

KEYNOTES:

#

1. THROUGH WALL PENETRATION FOR BACKBONE CONDUIT. OPTICAL FIBER CABLE CONTINUES ON CABLE TRAY TO RACKS.

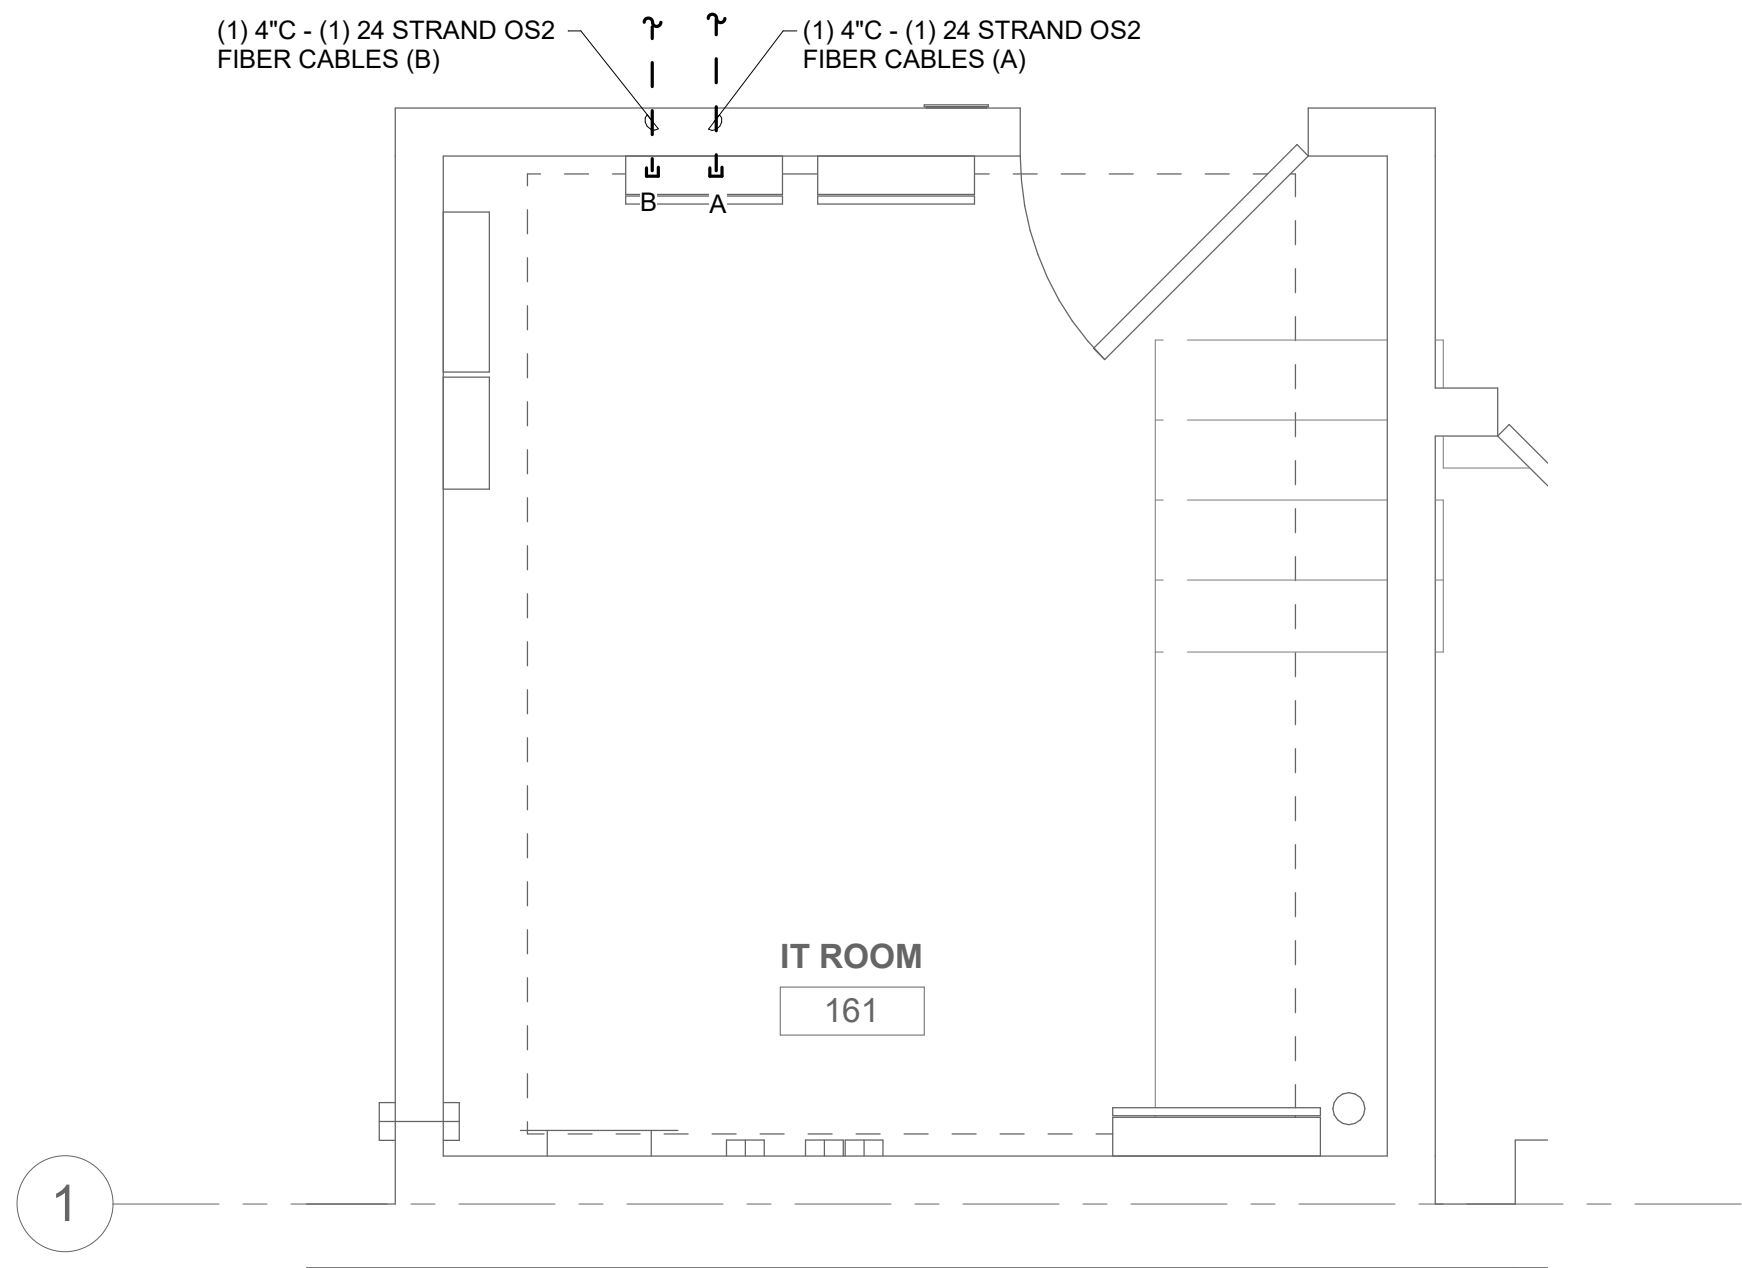


2

1/2" = 1'-0"

TELECOM ROOM PATHWAY PLAN - TR-173A-161

LEVEL 01

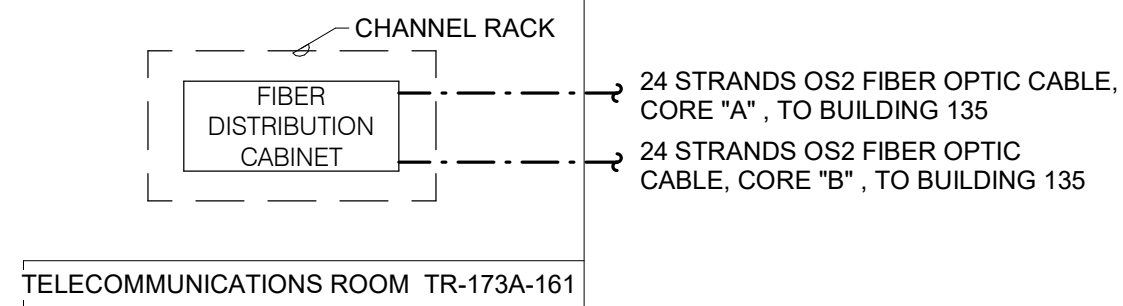

3

NO SCALE

FIBER RISER DIAGRAM

NOTES:

1. THIS RISER IS DIAGRAMMATIC AND MAY NOT SHOW ACTUAL ROUTING OR QUANTITIES OF MATERIALS SHOWN. THIS RISER IS SHOWN FOR CLARIFICATION OF CONNECTION(S), LOCATIONS AND CABLE TYPE. ALL INFORMATION OUTLETS ARE TYPICAL OF THE OUTLETS IN THE AREA SHOWN. REFER TO FLOOR PLANS FOR MORE SPECIFIC ROUTING INFORMATION. REFER TO SPECIFICATIONS FOR ADDITIONAL REQUIREMENTS.

2. REFER TO ELECTRICAL DRAWINGS FOR CHANNEL RACK AND FIBER OPTIC DISTRIBUTION CABINET SPECIFICATIONS

A

B

C

D

E

F

A

B

C

D


E

F


B:\M-360\509-22-700
VAHampton
E:\M-360\509-22-700\CAMPUS_1_P01.rvt

8/21/2025 6:24:18 AM


Revisions: Date:		CONSULTANT ENGINEERING DISCIPLINE:  225 W WASHINGTON STREET SUITE 2700 CHICAGO, IL 60609 P: 312.294.0501 F: 312.294.0003 PROJECT #22010109.00		ARCHITECT/ENGINEER OF RECORD A/E: SPEES DESIGN BUILD 23830 PACIFIC HIGHWAY S. SUITE 203 KENT, WA 98032 	STAMP 	Office of Construction and Facilities Management  U.S. Department of Veterans Affairs	Drawing Title TECHNOLOGY DETAILS Approved:	Phase 100% CONSTRUCTION DOCUMENTS FULLY SPRINKLERED	Project Title EHRM INFRASTRUCTURE UPGRADES - HAMPTON Location HAMPTON VA MEDICAL CENTER, HAMPTON, VIRGINIA Issue Date 05/09/2025 Checked EW Drawn IMEG	Project Number 509-22-700 Building Number Drawing Number T-400 710 of 713
--	--	--	--	--	---	--	---	--	--	---

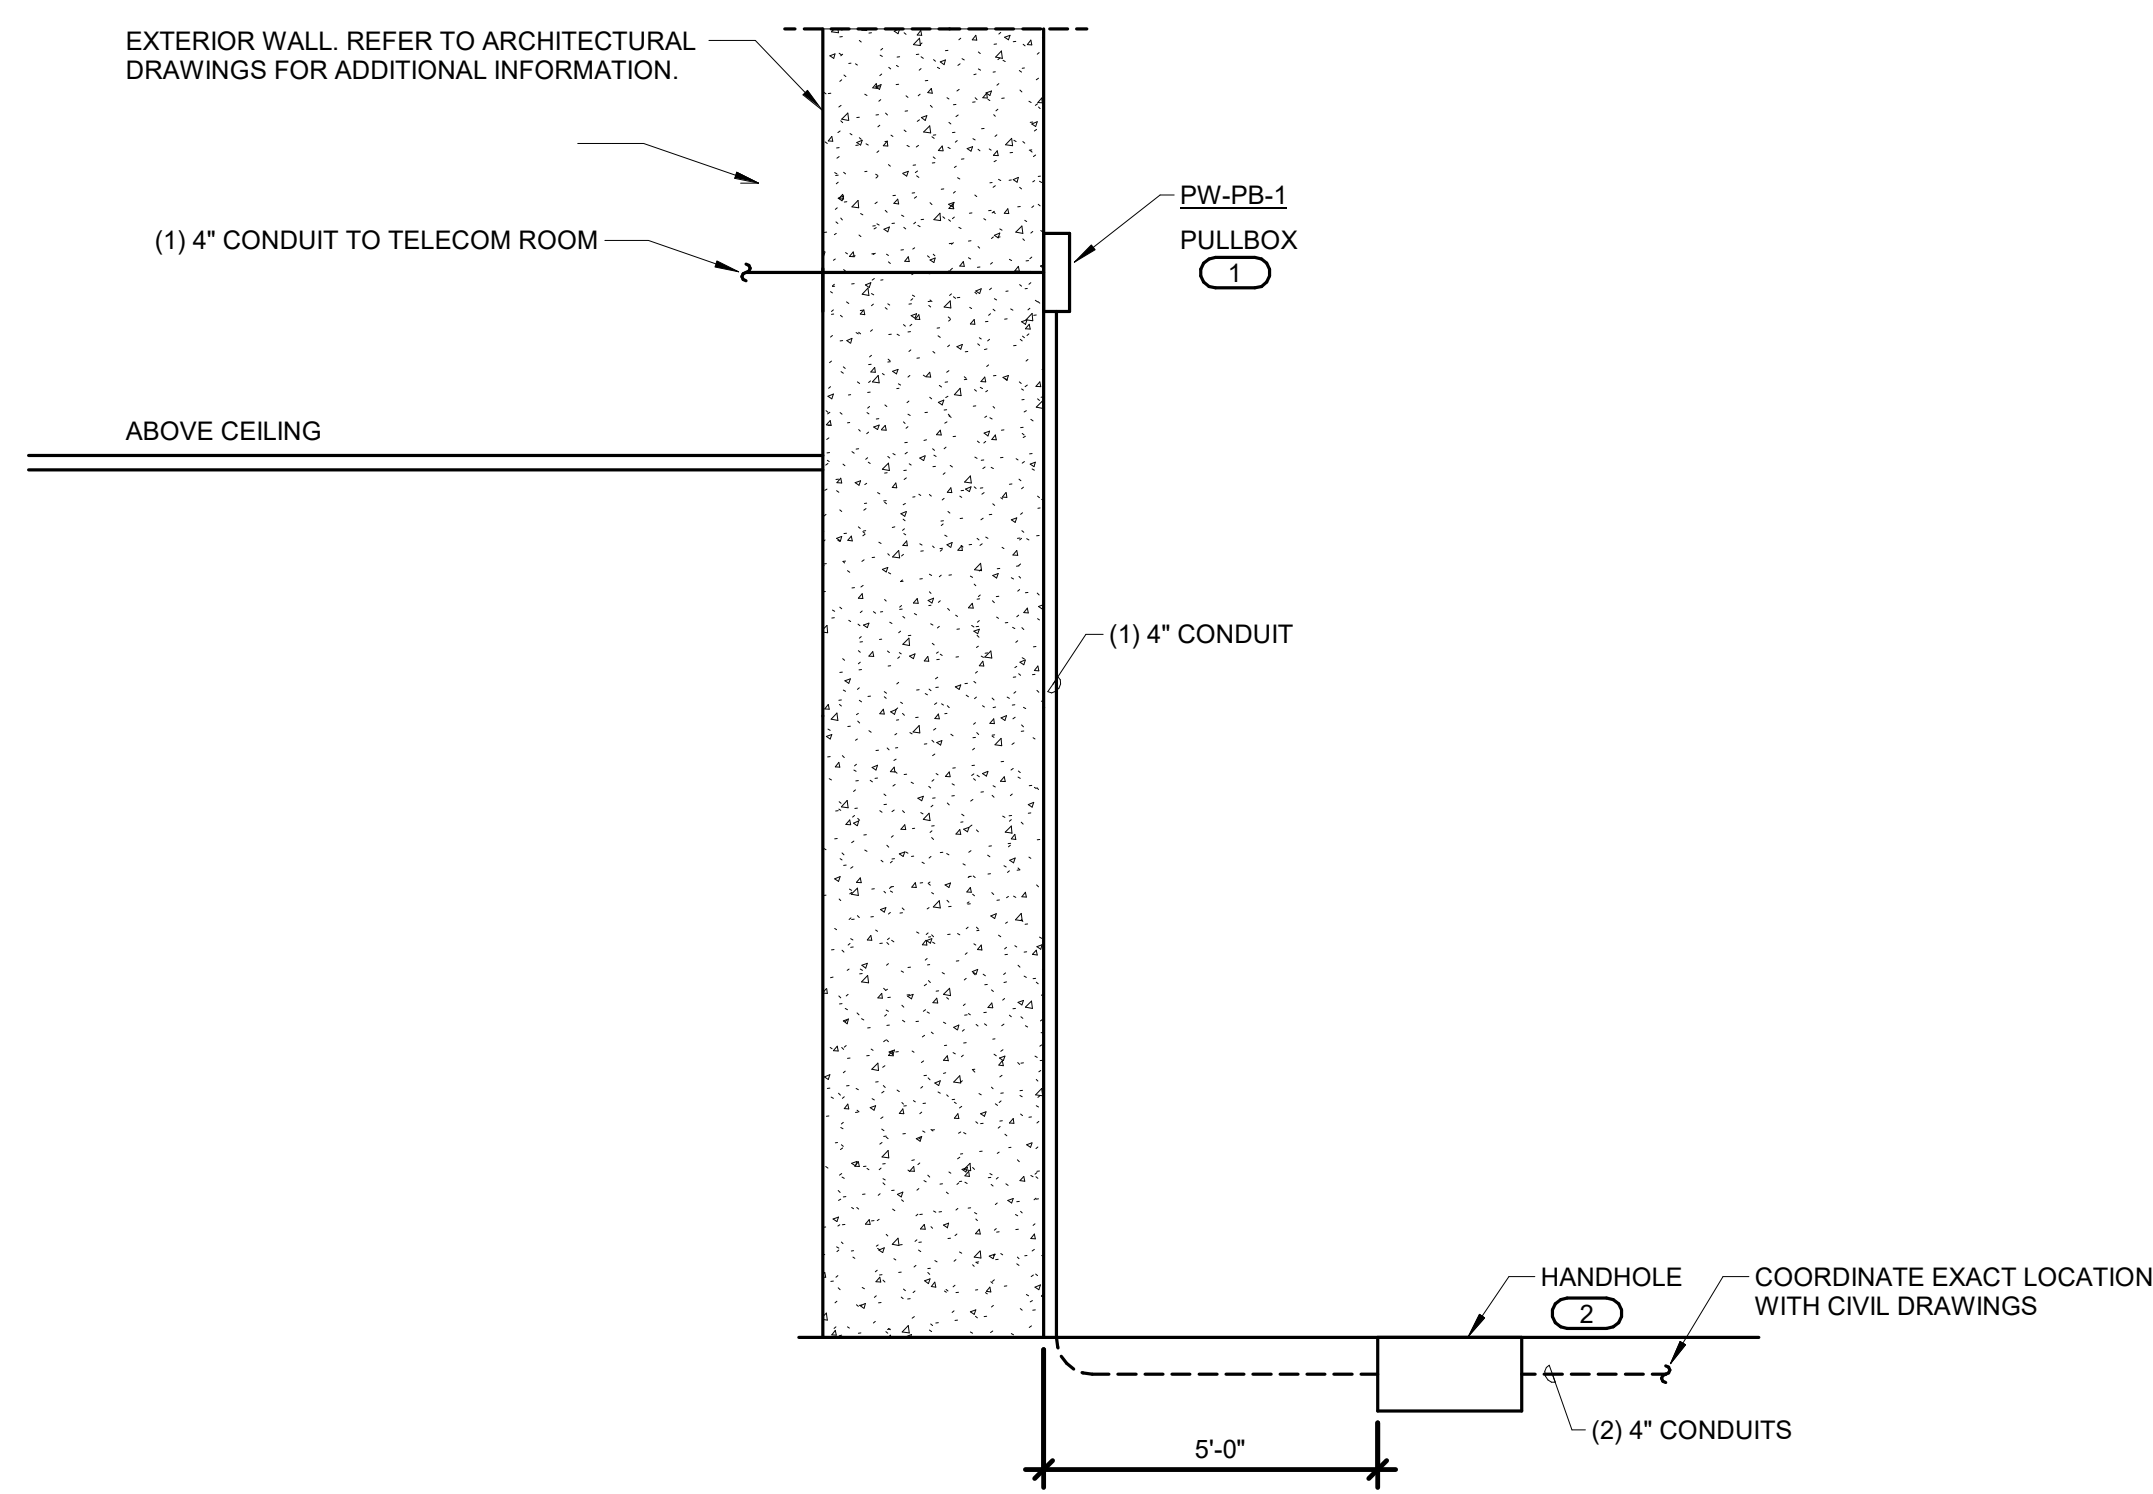


1 EXTERIOR PATHWAY DETAIL
NO SCALE
NOTES:
1. REFER TO CIVIL DRAWINGS FOR EXACT LOCATION OF HANDHOLES.
KEYNOTES: **#**
1. CONTRACTOR SHALL FIELD VERIFY PULLBOX ELEVATION TO ROUTE CONDUITS INTO BUILDING ABOVE FINISHED CEILING.
2. REFER TO 2/T400 EXTERIOR HAND HOLE DETAIL FOR ADDITIONAL INFORMATION.

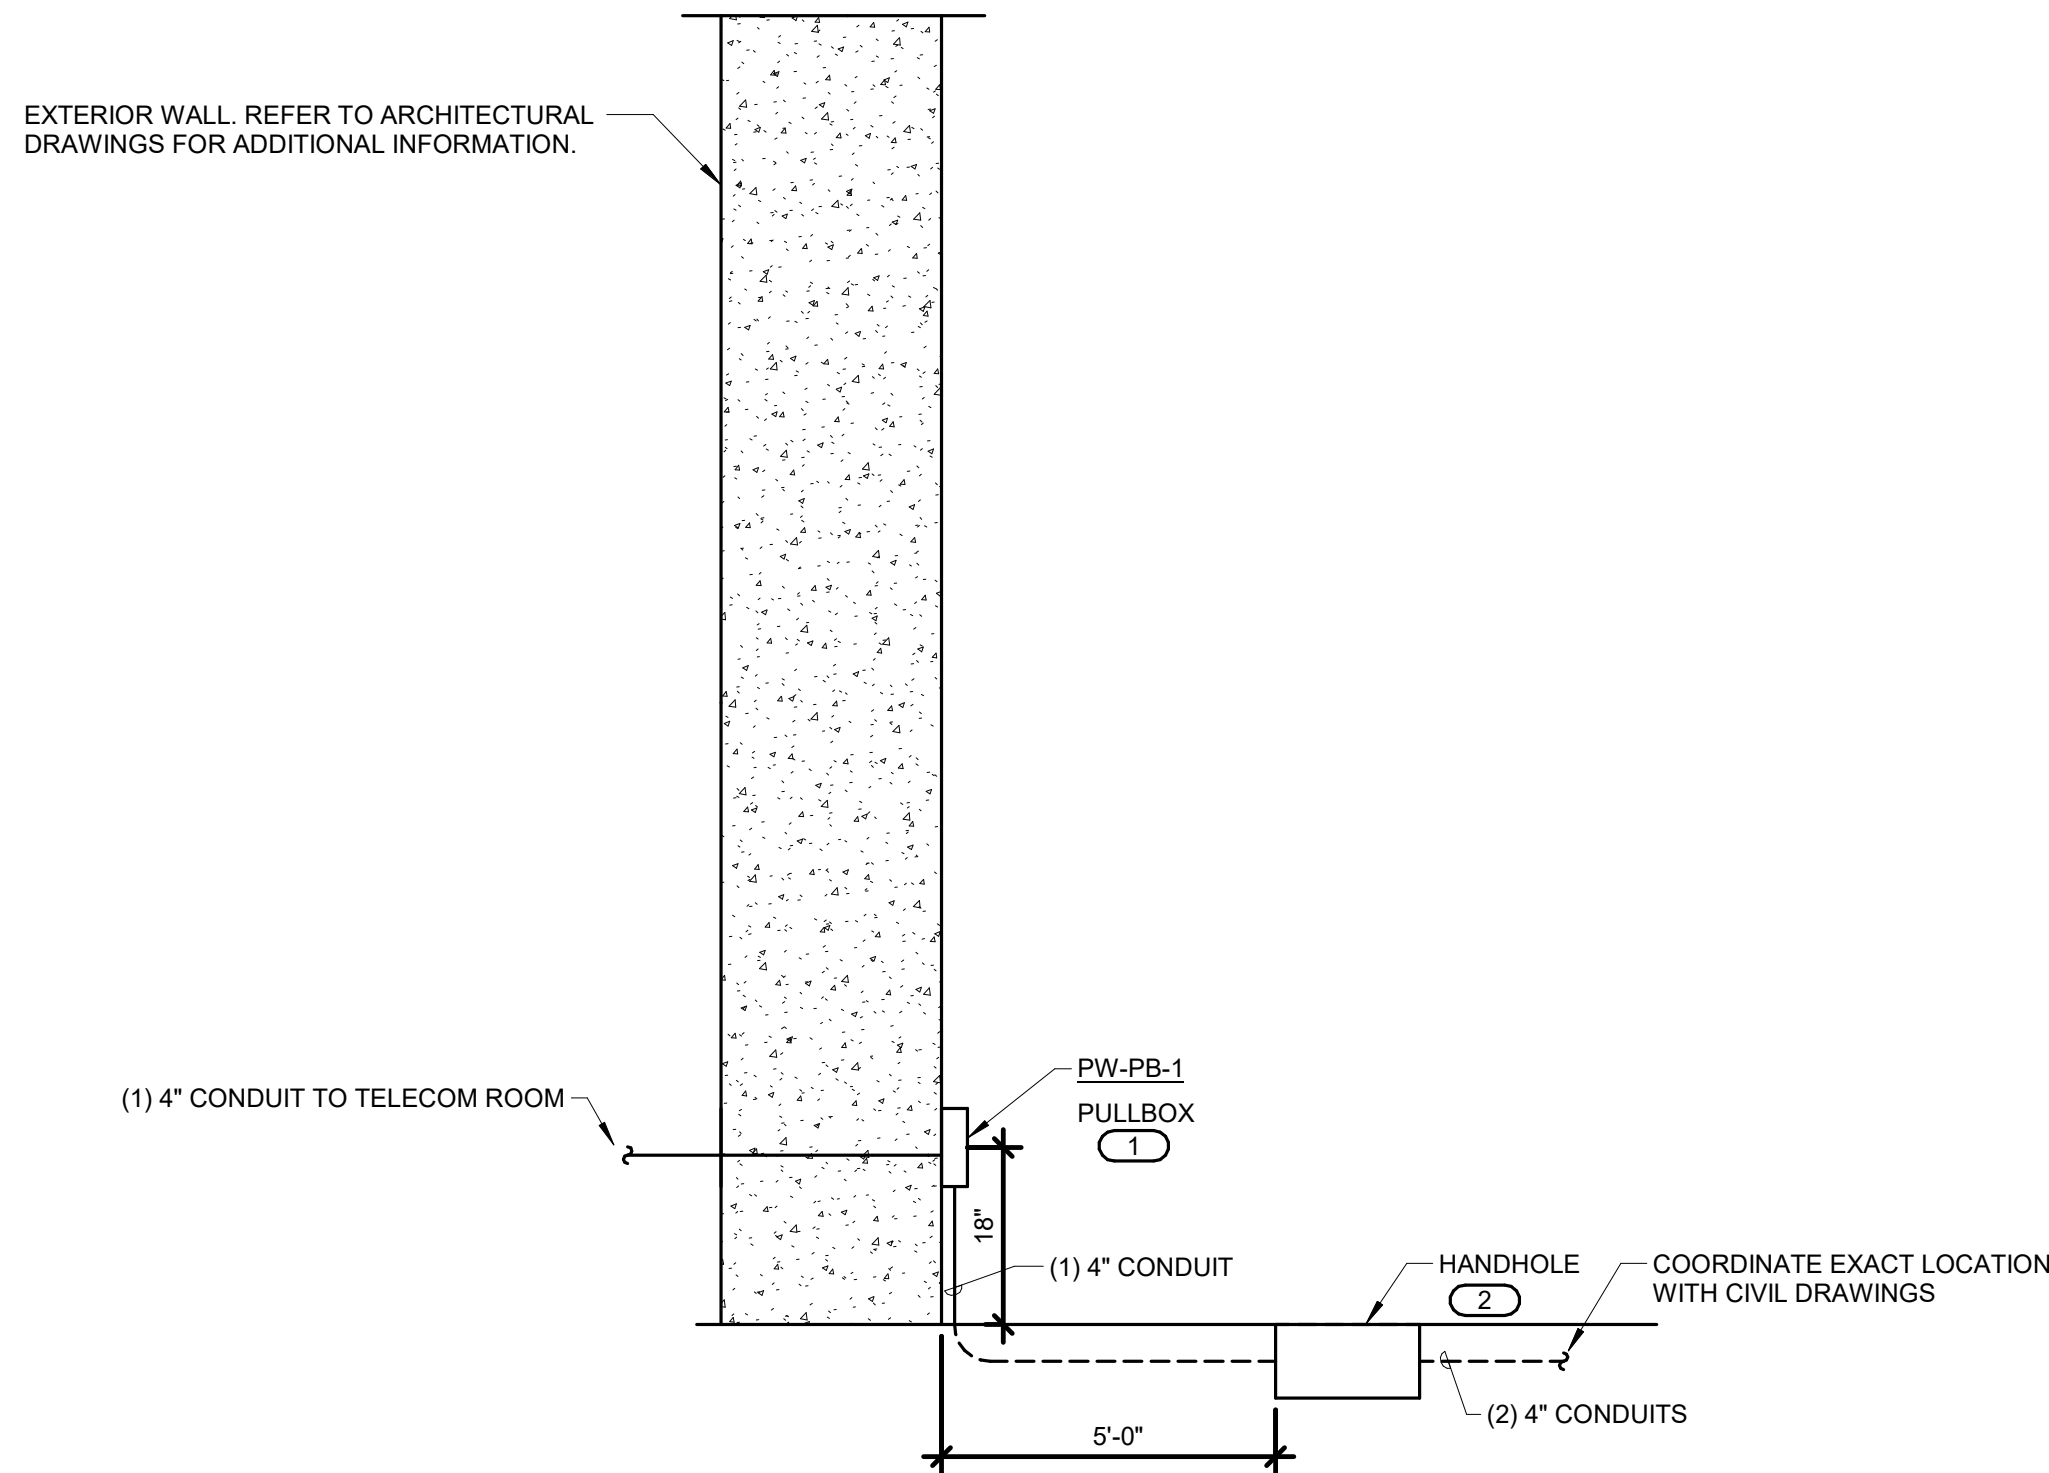

2 EXTERIOR PATHWAY DETAIL (LOW HEIGHT)
NO SCALE
NOTES:
1. REFER TO CIVIL DRAWINGS FOR EXACT LOCATION OF HANDHOLES.
KEYNOTES: **#**
1. CONTRACTOR TO COORDINATE JUNCTION BOX ELEVATIONS.
2. REFER TO 2/T400 EXTERIOR HAND HOLE DETAIL FOR ADDITIONAL INFORMATION.

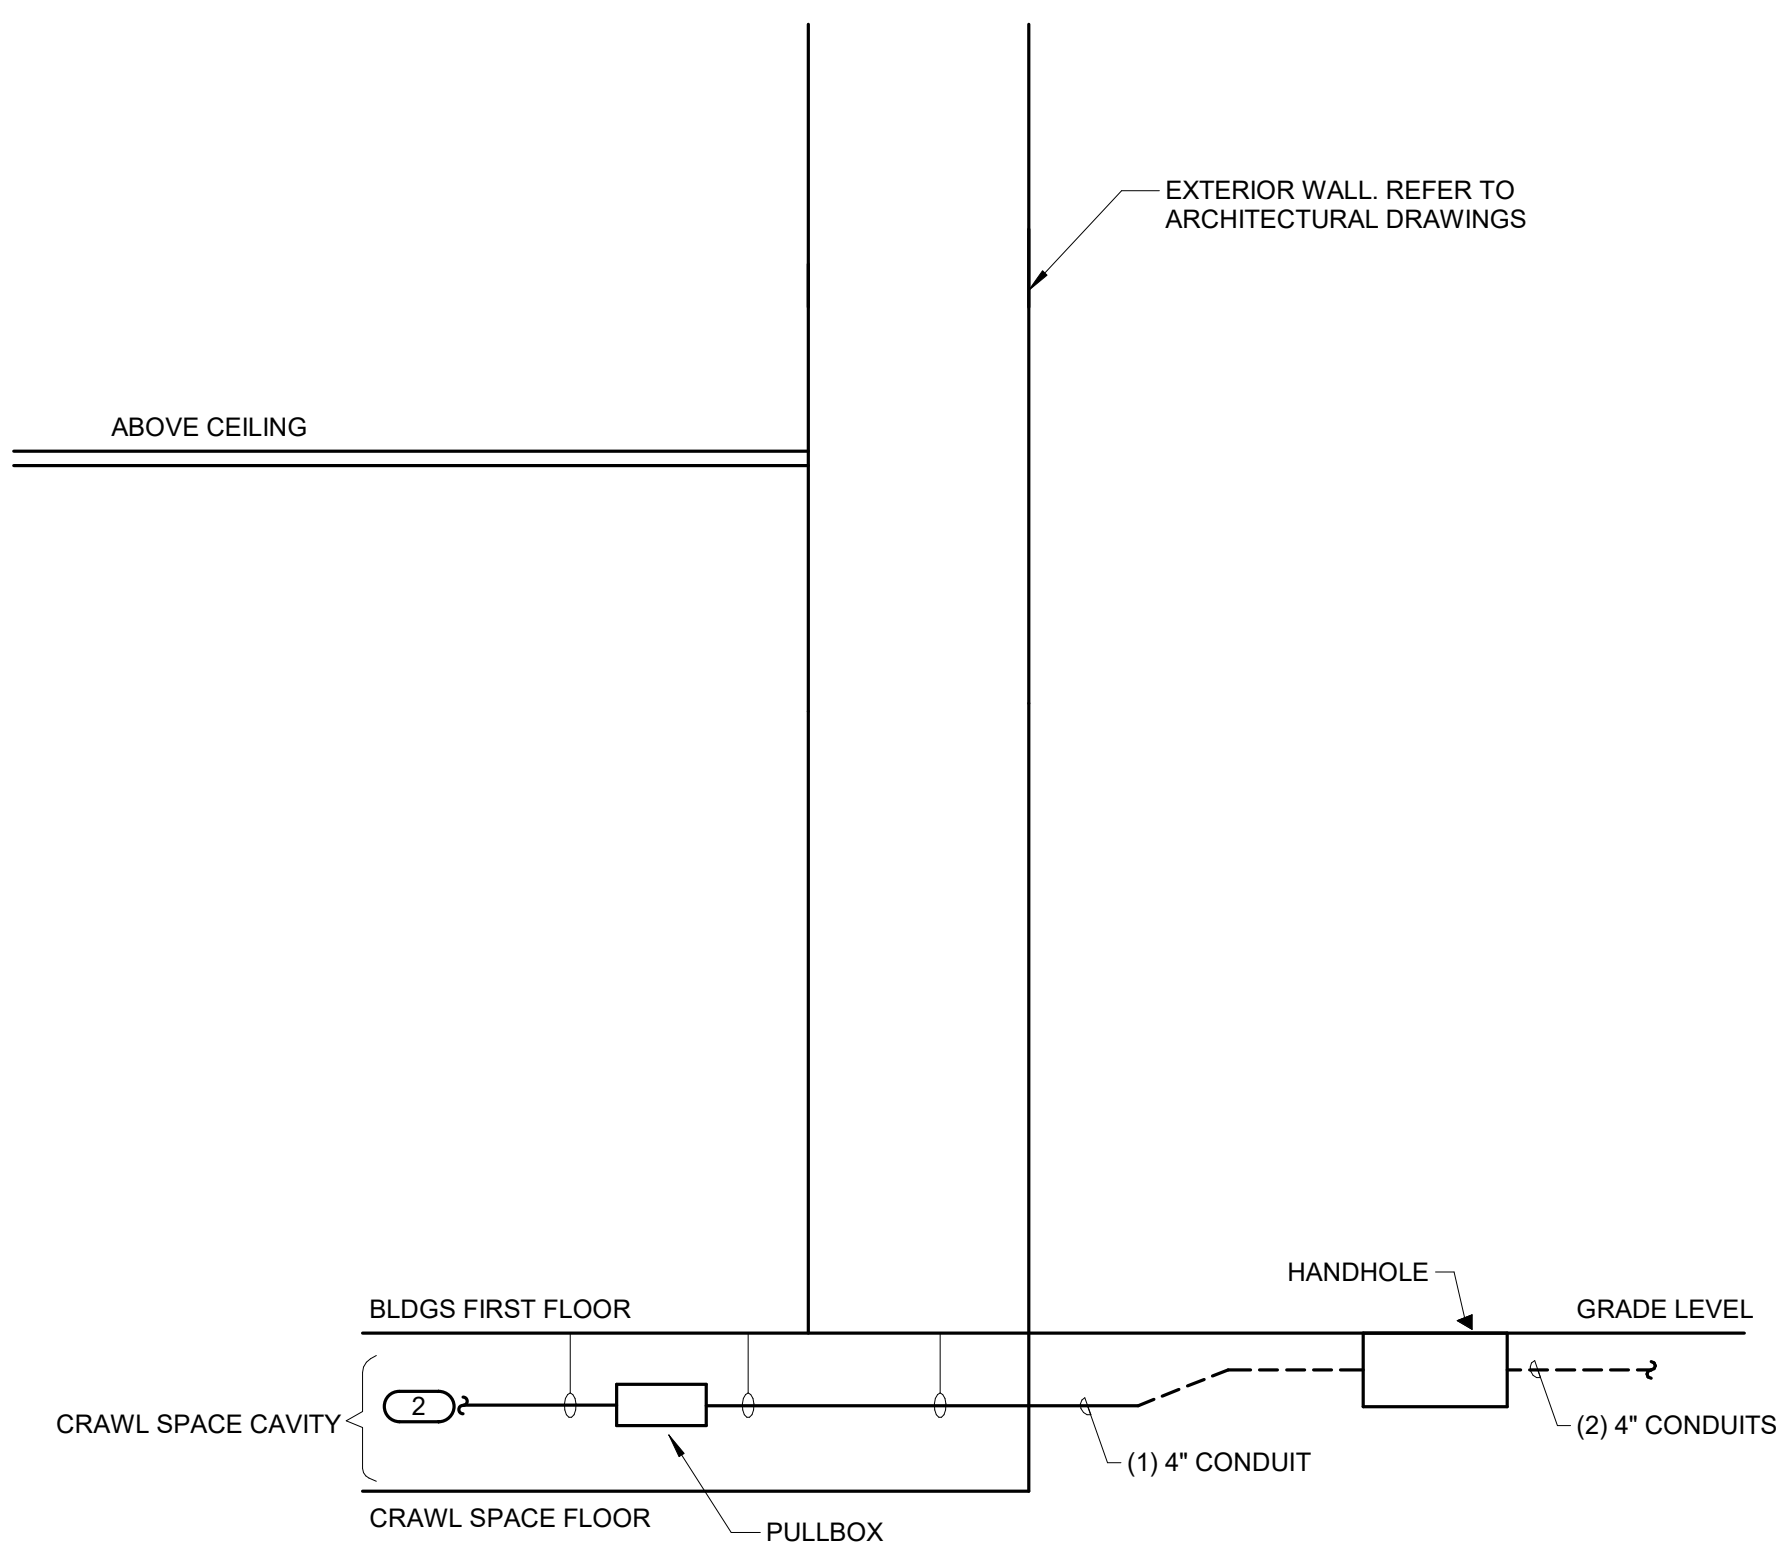

3 EXTERIOR PATHWAY DETAIL (CRAWL SPACE)
NO SCALE
KEYNOTES:
1. ROUTE CONDUITS THROUGH CRAWL SPACES SUSPENDED ABOVE FLOOR AND SUPPORTED BY BEAM CLAMPS, PIPE COLLARS AND SPACERS.
2. ROUTE CONDUIT THROUGH CRAWL SPACE TO CONDUIT STUB UP LOCATION. REFER TO INTERIOR FLOOR PLANS FOR STUB UP LOCATIONS.

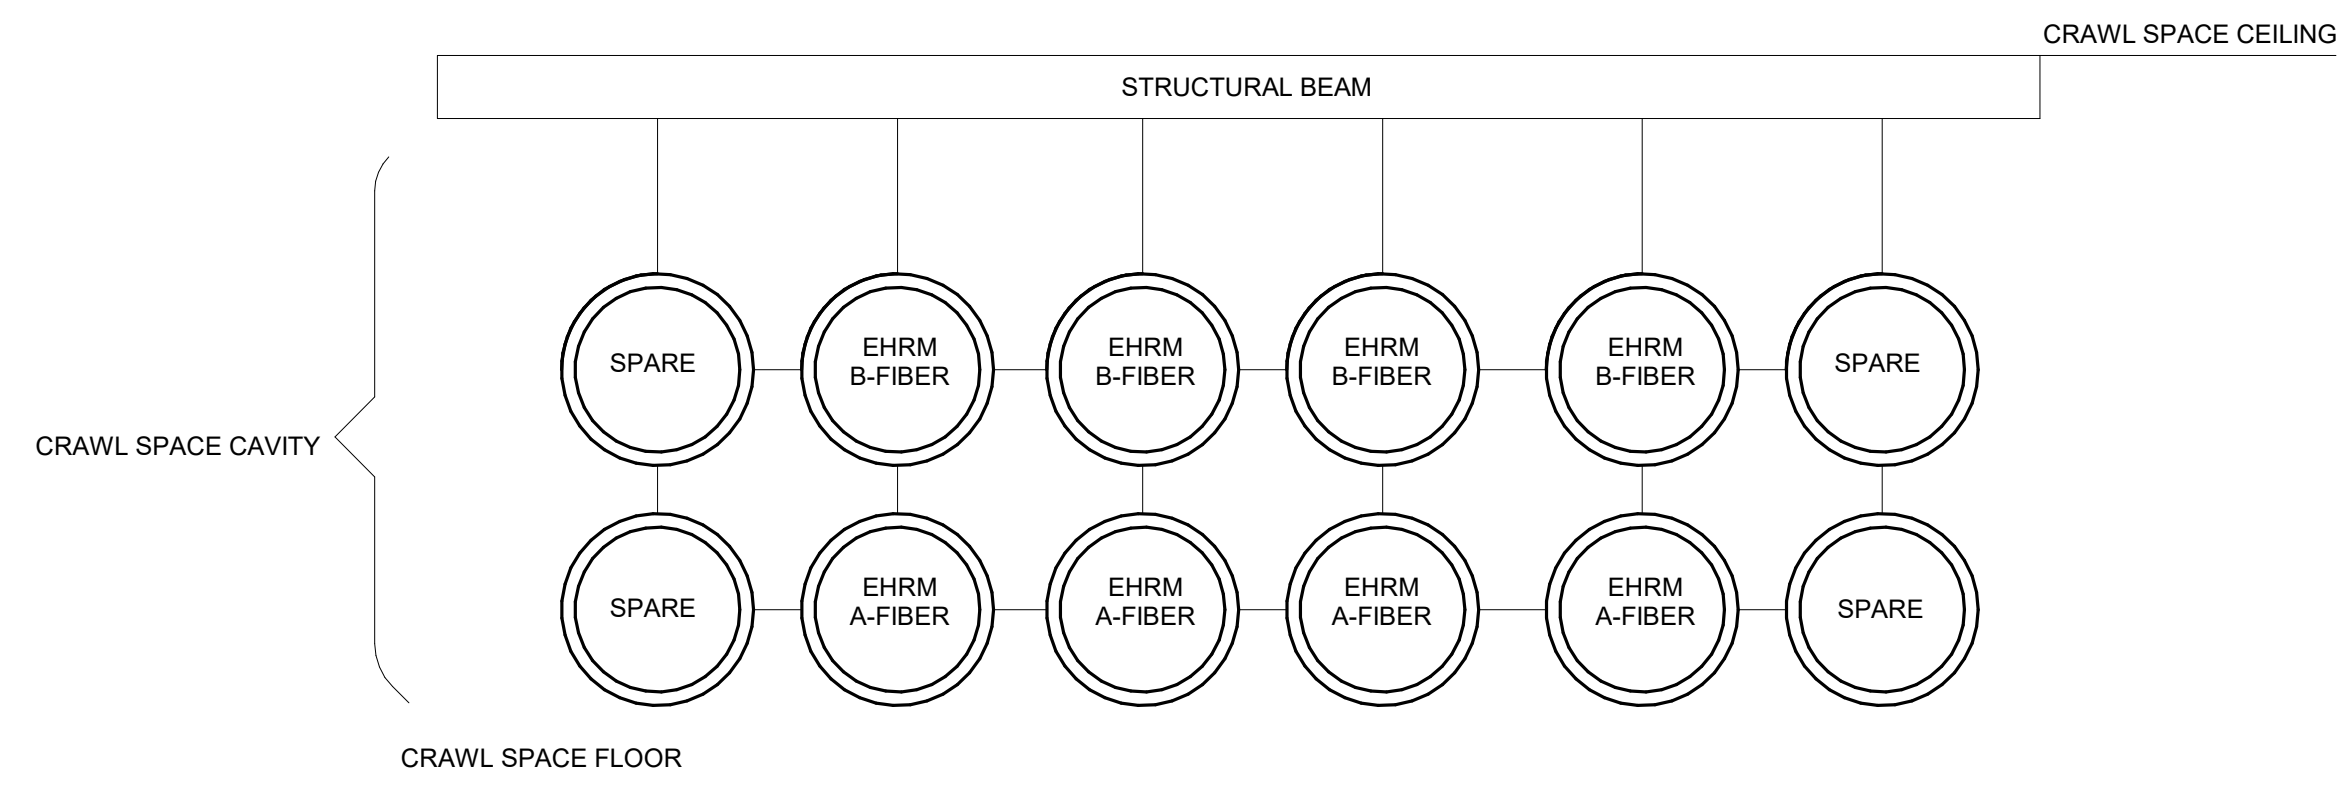

4 EXTERIOR PATHWAY DETAIL (BLDG 146 CRAWL SPACE SECTION)
NO SCALE
NOTES:
1. ROUTE CONDUITS THROUGH CRAWL SPACES SUSPENDED ABOVE FLOOR AND SUPPORTED BY BEAM CLAMPS, PIPE COLLARS AND SPACERS.
2. IN BLDG 146 CRAWL SPACE, ROUTE CONDUIT IN A (2) x (6) CONDUIT STACK. ADJUST CONDUIT ARRANGEMENT TO (1) x (12) OR (3) x (4) CONDUIT STACK AS REQUIRED TO ROUTE THROUGH CRAWL SPACE.

		CONSULTANT	ARCHITECT/ENGINEER OF RECORD	STAMP REGISTERED COMMUNICATIONS DISTRIBUTION DESIGNER Bicsi Eddie C. Wiles, Jr. Reg. No. 151950R EXPIRES 12-31-2025 RCDD <i>E. Wiles</i>	Office of Construction and Facilities Management VAU.S. Department of Veterans Affairs	Drawing Title	Phase	Project Title	Project Number
		ENGINEERING DISCIPLINE:	A/E:			TECHNOLOGY DETAILS	100% CONSTRUCTION DOCUMENTS	EHRM INFRASTRUCTURE UPGRADES - HAMPTON	509-22-700
		IMEG www.imegcorp.com 225 W WASHINGTON STREET SUITE 2700 CHICAGO, IL 60606 P: 312.294.0501 F: 312.294.0003 PROJECT #22010109.00	SDB SPEESDESIGNBUILD 23830 PACIFIC HIGHWAY S. SUITE 203 KENT, WA 98032			Approved:	FULLY SPRINKLERED	Location	Building Number
								HAMPTON VA MEDICAL CENTER, HAMPTON, VIRGINIA	
		Revisions:	Date:					Issue Date	Checked
				05/09/2025	EW	IMEG	T-401 711 of 713		

A


B

C

D

E

F

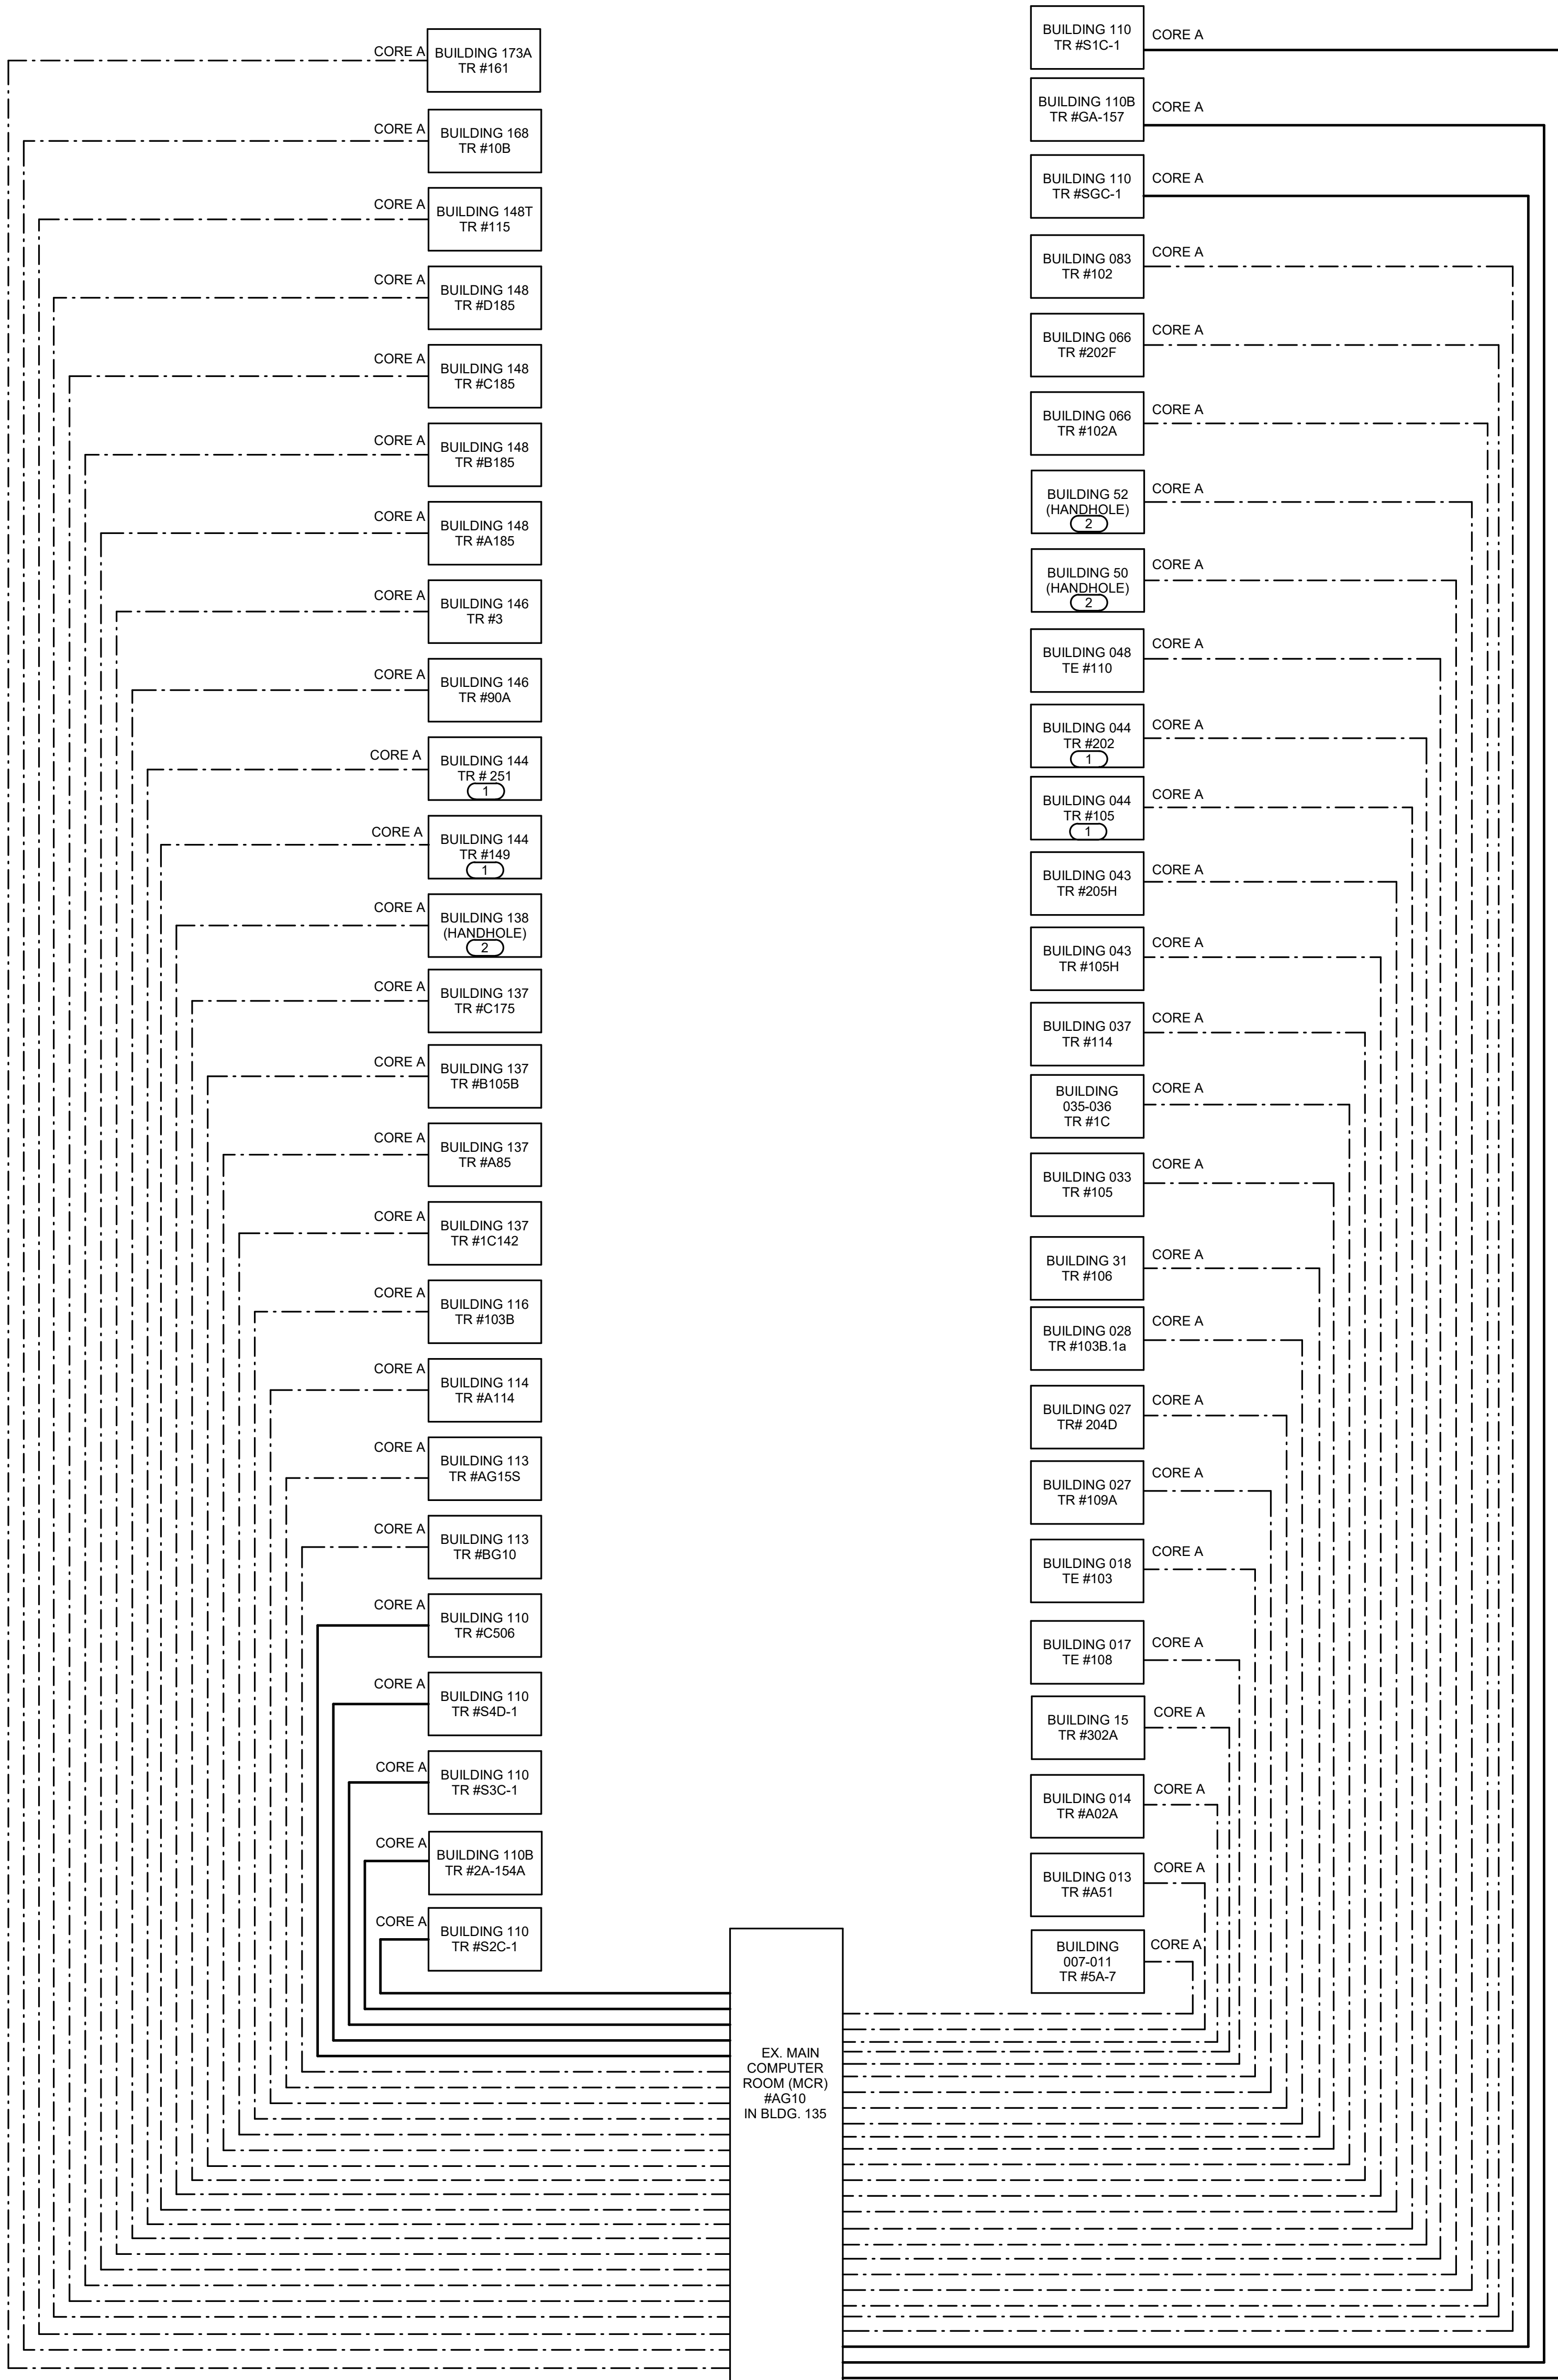

1

SITE FIBER RISER DIAGRAM - CORE A

NO SCALE

- NOTES:
- THIS RISER IS DIAGRAMMATIC AND MAY NOT SHOW ACTUAL ROUTING OR QUANTITIES OF MATERIALS SHOWN. THIS RISER IS SHOWN FOR CLARIFICATION OF CONNECTION(S), LOCATIONS AND CABLE TYPE. REFER TO RISER DIAGRAMS OF INDIVIDUAL BUILDINGS FOR ADDITIONAL INFORMATION. REFER TO FLOOR PLANS AND SITE PLAN FOR MORE SPECIFIC ROUTING INFORMATION. REFER TO SPECIFICATIONS FOR ADDITIONAL REQUIREMENTS.
 - SOLID LINE REPRESENTS 24 STRANDS OM4 AND 12 STRANDS OS1 HYBRID FIBER OPTIC CABLE, CORE "A".
 - DASHED LINE REPRESENTS 24 STRANDS OS2 FIBER OPTIC CABLE, CORE "A".
- KEYNOTES:
- BUILDINGS #44 AND #144 TELECOM ROOMS (TR) ARE EXISTING TO REMAIN. T.C. SHALL PROVIDE NEW OPTICAL FIBER CABLES AS INDICATED. ROUTE FIBER TO EXISTING FIBER DISTRIBUTION HOUSING IN EXISTING RACK. TERMINATE OPTICAL FIBER CABLES WITH NEW LC CASSETTES.
 - NEW BUILDINGS ARE BEING CONSTRUCTED FOR EXISTING BUILDINGS 50, 52 AND 138. CONTRACTOR SHALL COIL NEW FIBER BACKBONE CABLES IN WEATHERPROOF BAG OR MATERIAL IN NEW HANDHOLES NEAR EXISTING BUILDINGS. NEW FIBER BACKBONE CABLES SHALL BE ROUTE TO TR IN, RESPECTIVE, NEW BUILDINGS AND TERMINATED UNDER A SEPARATE CONTRACT.

A


B

C

D

E

F

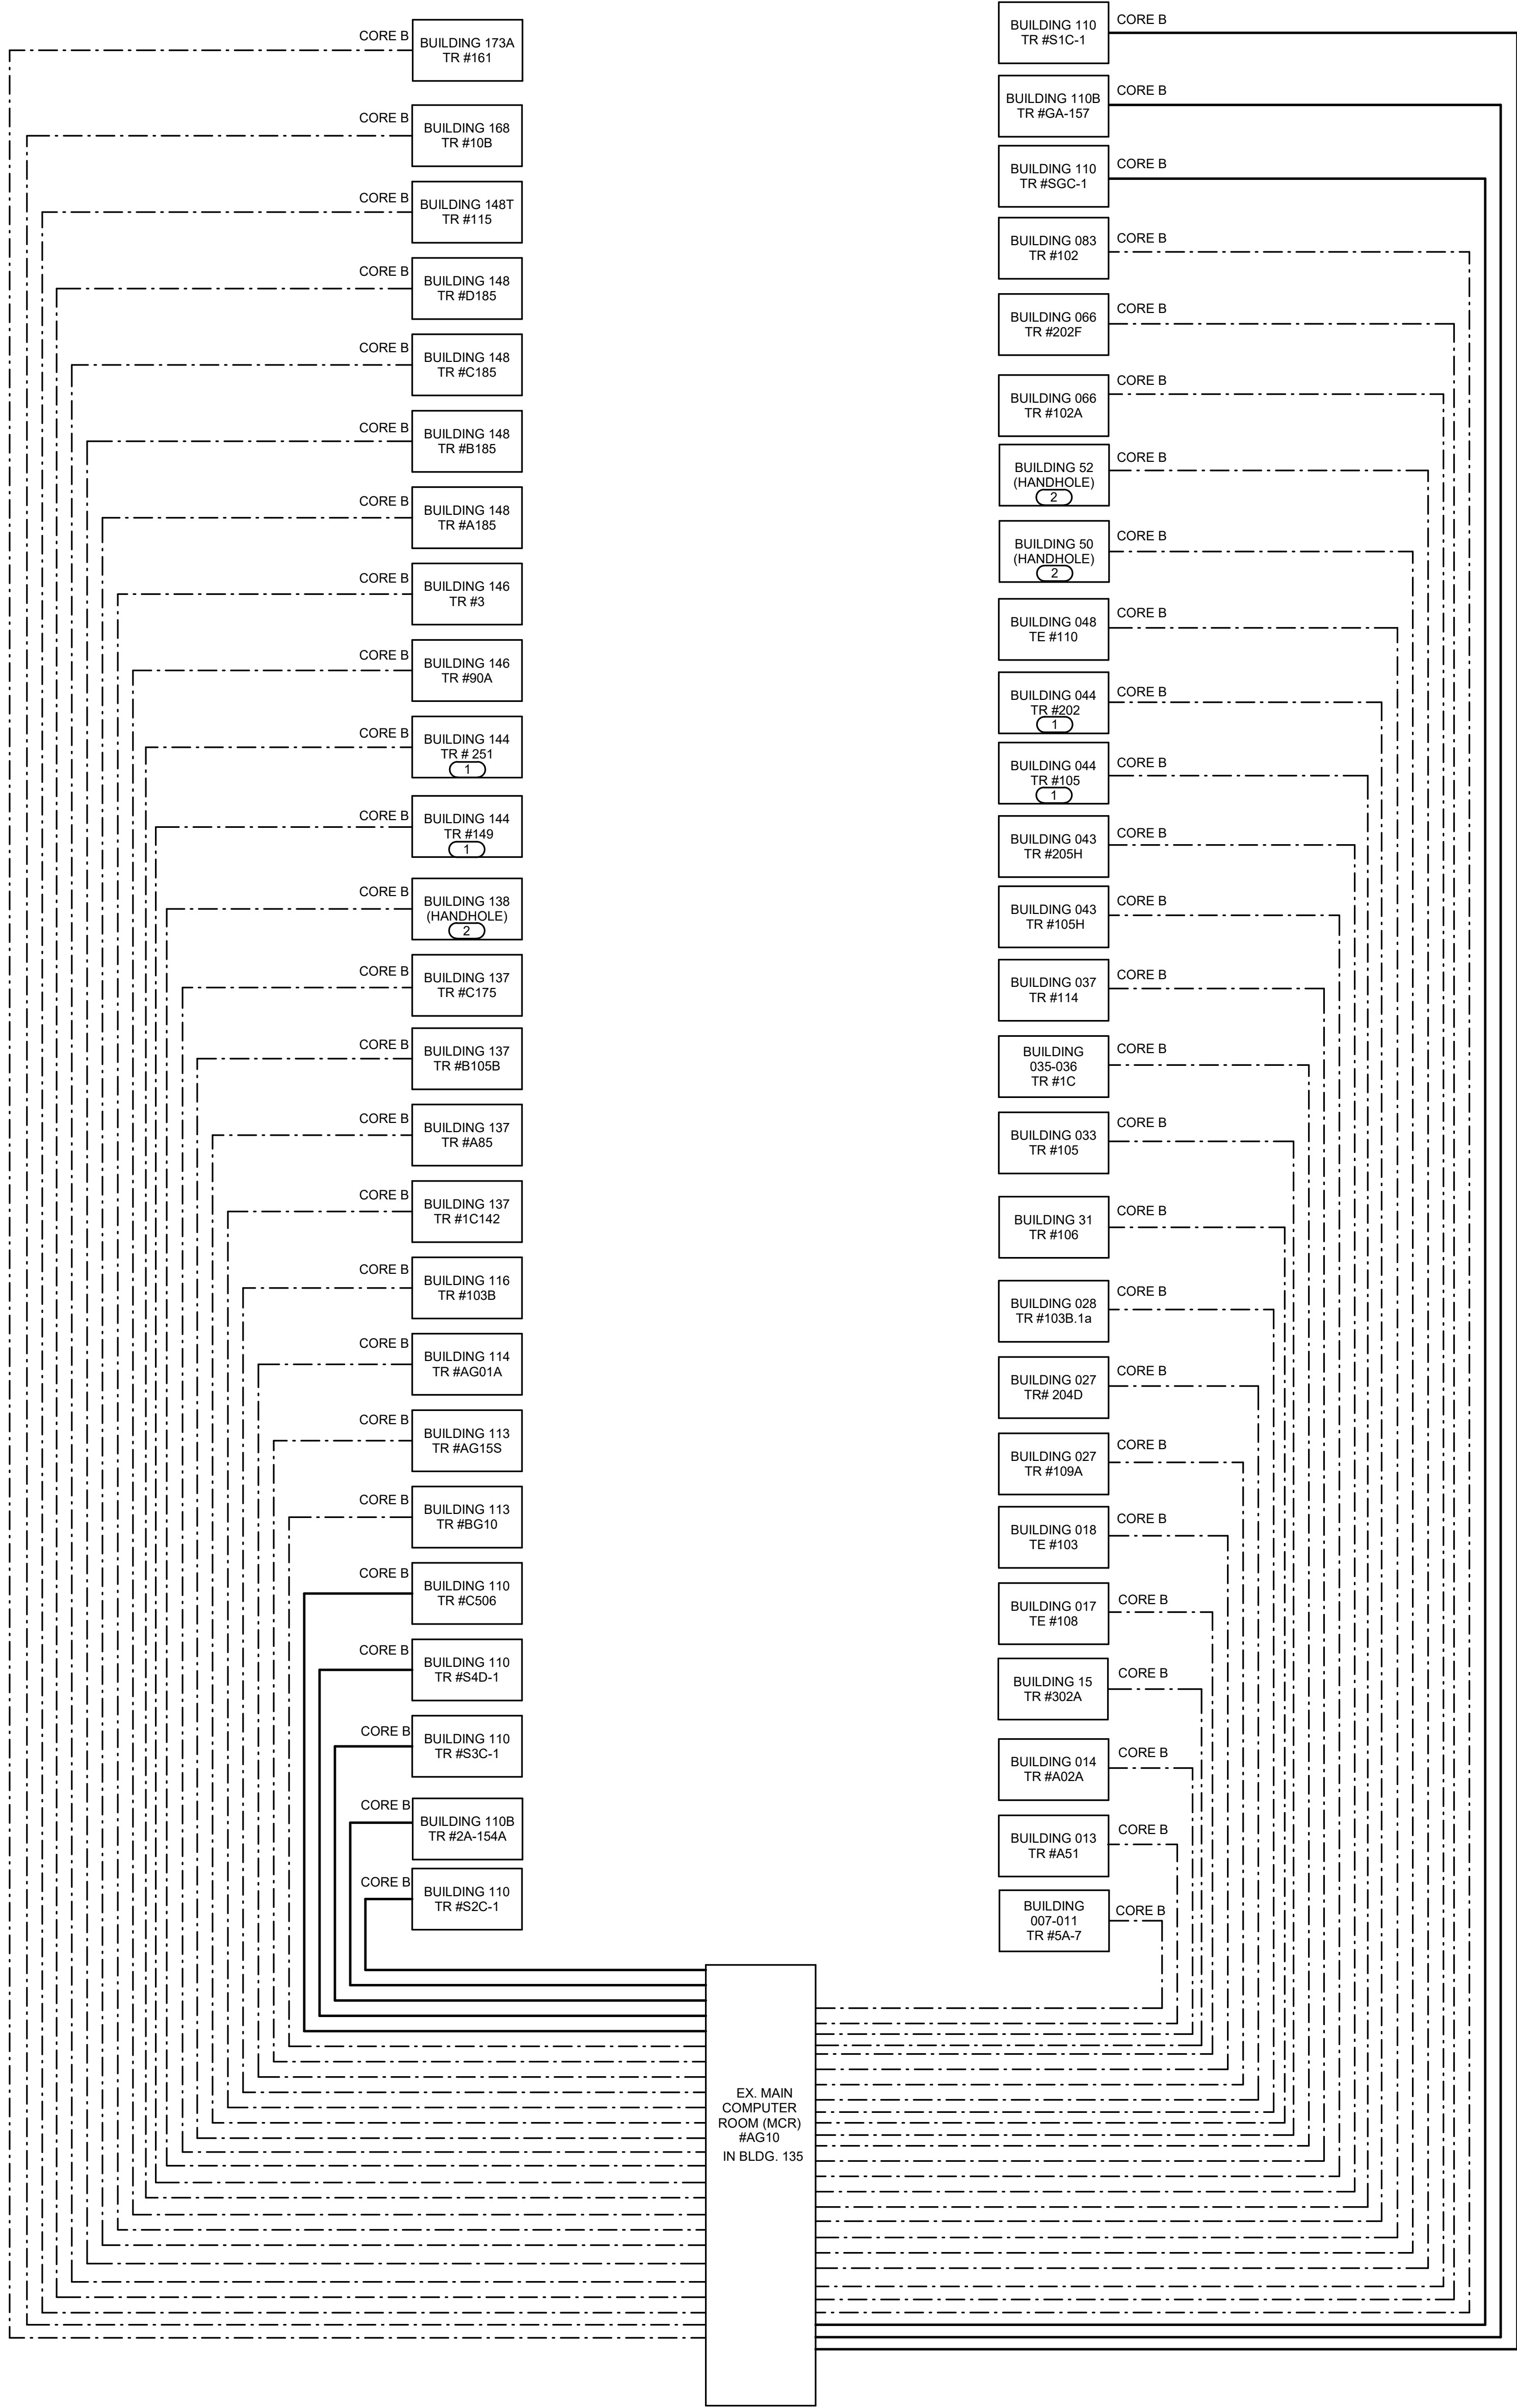

1

SITE FIBER RISER DIAGRAM - CORE B

NO SCALE

NOTES:

- THIS RISER IS DIAGRAMMATIC AND MAY NOT SHOW ACTUAL ROUTING OR QUANTITIES OF MATERIALS SHOWN. THIS RISER IS SHOWN FOR CLARIFICATION OF CONNECTIONS, LOCATIONS AND CABLE TYPE. REFER TO RISER DIAGRAMS OF INDIVIDUAL BUILDINGS FOR ADDITIONAL INFORMATION. REFER TO FLOOR PLANS AND SITE PLAN FOR MORE SPECIFIC ROUTING INFORMATION. REFER TO SPECIFICATIONS FOR ADDITIONAL REQUIREMENTS.
- SOLID LINE REPRESENTS 24 STRANDS OM4 AND 12 STRANDS OS1 HYBRID FIBER OPTIC CABLE, CORE "B".
- DASHED LINE REPRESENTS 24 STRANDS OS2 FIBER OPTIC CABLE, CORE "B".

KEYNOTES:

- BUILDINGS #44 AND #144 TELECOM ROOMS (TR) ARE EXISTING TO REMAIN. T.C. SHALL PROVIDE NEW OPTICAL FIBER CABLES AS INDICATED. ROUTE CABLES TO EXISTING FIBER DISTRIBUTION HOUSING IN EXISTING RACK. TERMINATE OPTICAL FIBER CABLES WITH NEW I.C. CASSETTES.
- NEW BUILDINGS ARE BEING CONSTRUCTED FOR EXISTING BUILDINGS 50, 52 AND 138. CONTRACTOR SHALL COIL NEW FIBER BACKBONE CABLES IN WEATHERPROOF BAG OR MATERIAL IN NEW HANDHOLES NEAR EXISTING BUILDING. NEW FIBER BACKBONE CABLES SHALL BE ROUTE TO TR IN , RESPECTIVE, NEW BUILDINGS AND TERMINATED UNDER A SEPARATE CONTRACT.

--	--	