



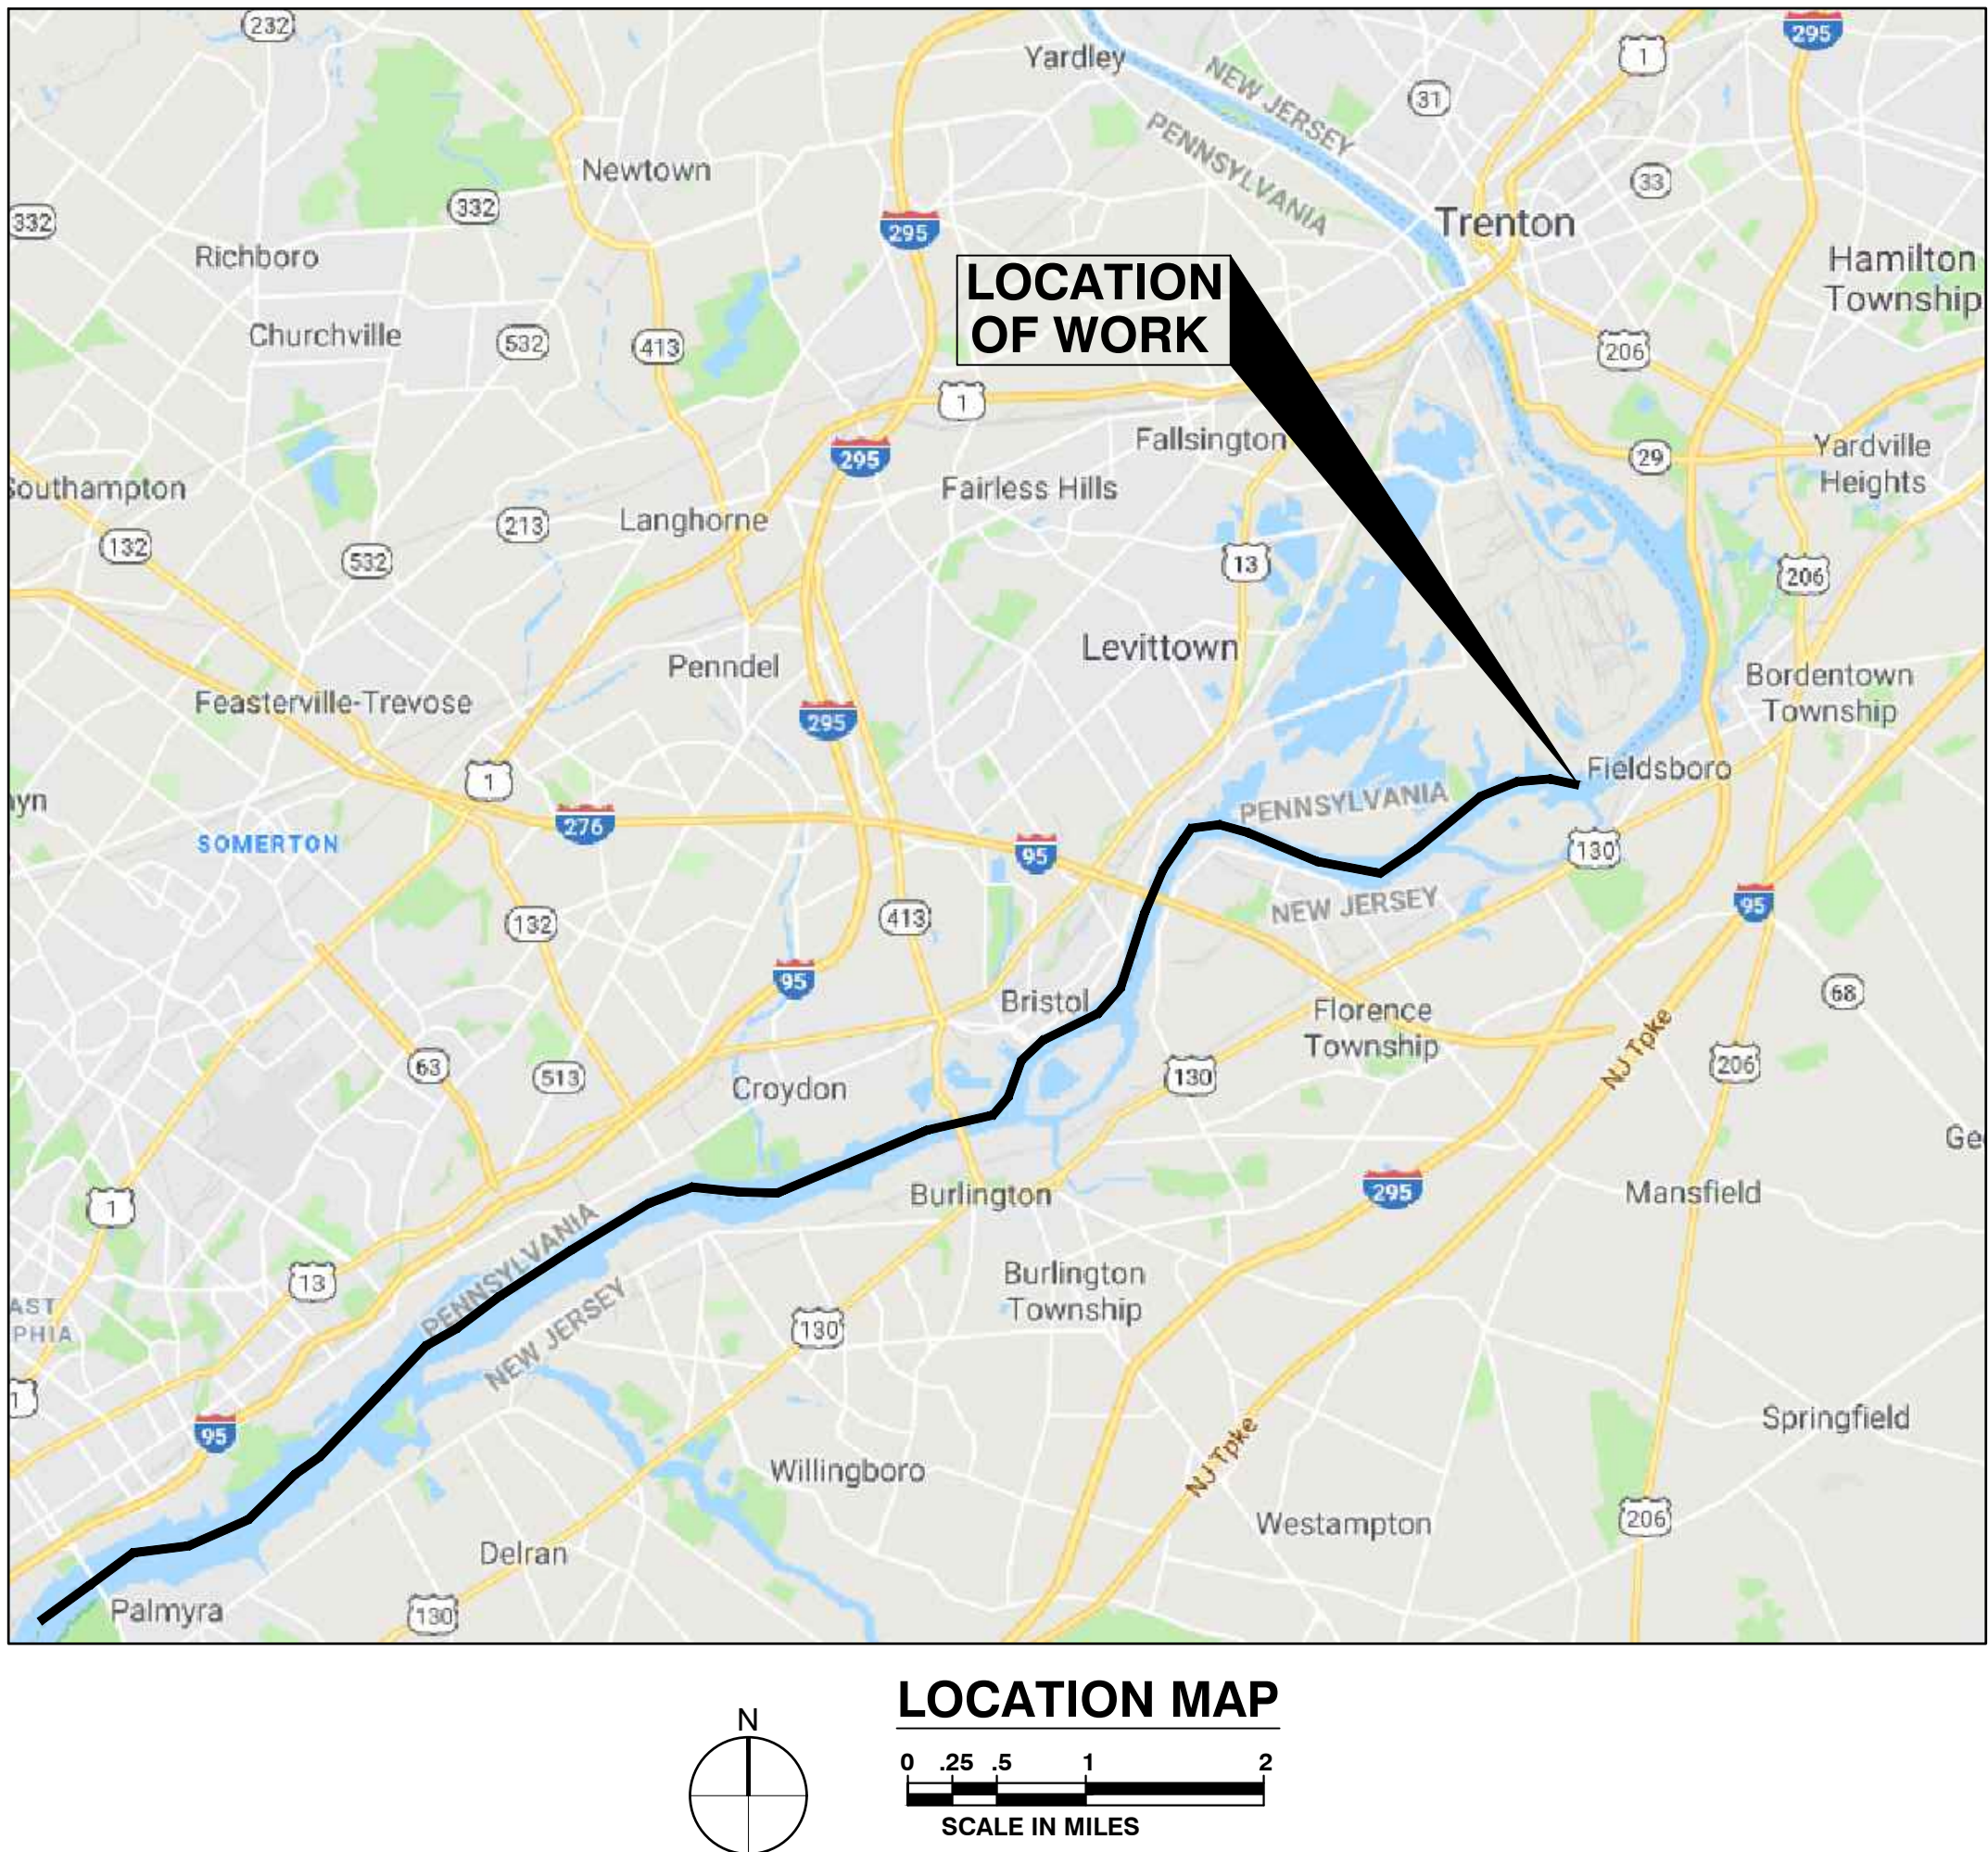

**US Army Corps **
of Engineers
PHILADELPHIA
DISTRICT

MAINTENANCE DREDGING
-
DELAWARE RIVER
PHILADELPHIA, PENNSYLVANIA TO TRENTON, NEW JERSEY

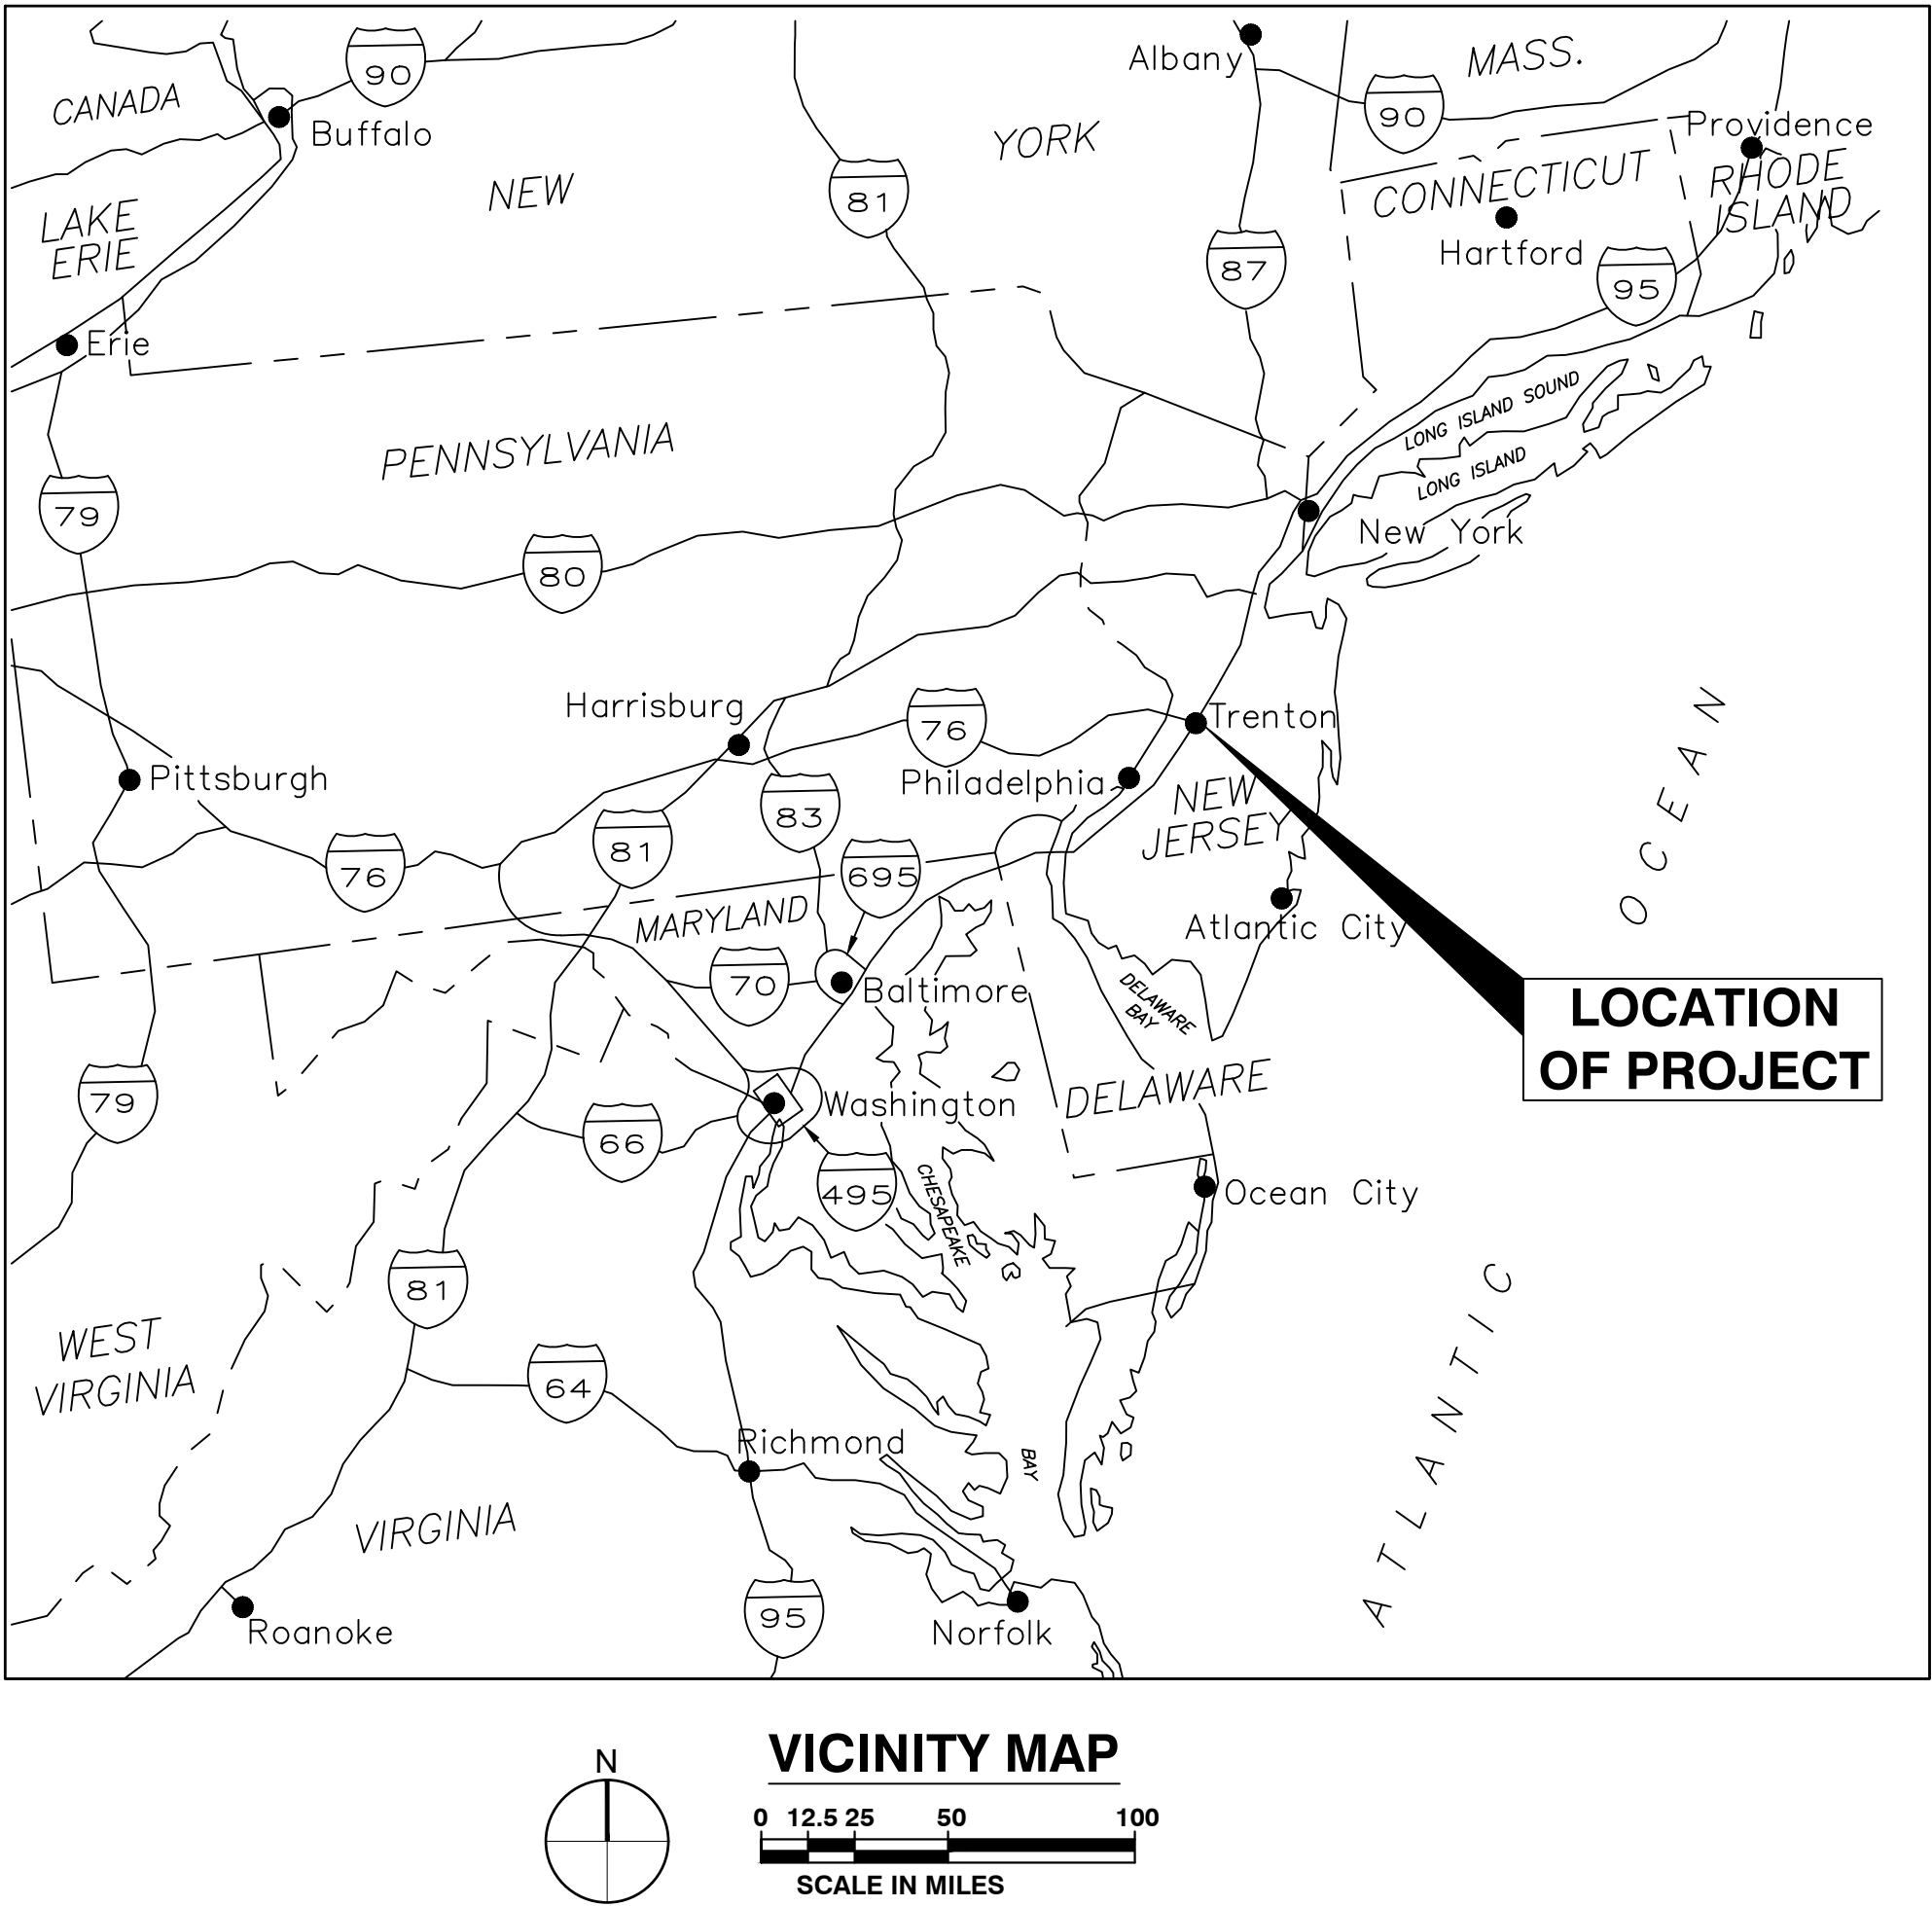

SOLICITATION NO:W912BU25BA008
CONTRACT NO:-
ISSUE/SUBMITTAL DATE:JUNE 2025

THIS PROJECT WAS DESIGNED BY THE PHILADELPHIA DISTRICT OF THE U.S. ARMY CORPS OF ENGINEERS. THE INITIALS OR SIGNATURES AND REGISTRATION DESIGNATIONS OF INDIVIDUALS APPEAR ON THESE PROJECT DOCUMENTS WITHIN THE SCOPE OF THEIR EMPLOYMENT AS REQUIRED BY ER 1110-1-8152.	SUBMITTED:
	TRAVIS T. FATZINGER, P.E. CHIEF, ENGINEERING BRANCH
	APPROVED:
	ANDREW J. SCHWAIGER, P.E. CHIEF, ENGINEERING AND CONSTRUCTION DIVISION

[illegible]

U.S. ARMY CORPS OF ENGINEERS PHILADELPHIA DISTRICT	DESIGNED BY:	L.MULVILL	ISSUED/REMITTAL DATE:	JUNE 2025
	DRAWN BY:		SOLICITATION NUMBER:	
	CHECKED BY:		CONTRACT NUMBER:	
	O.D.R.#	-	PLOT DATE:	
	SUBMITTED BY:	T.HAZENGER	FILE NAME:	
	ANSI Z39-48	ISO COVER SHEET 2nd		

DELAWARE RIVER
PHILADELPHIA, PENNSYLVANIA TO TRENTON, NEW JERSEY
MAINTENANCE DREDGING
COVER SHEET

SHEET ID
G-001

	1	2	3	4	5	6	7	8	9	10	11	12	13	14	15	16	17	18	19	20	21	22	23	24	25	26	27
X																											
V																											
U																											
T																											
S																											
R																											
Q																											
P																											
O																											
N																											
M																											
L																											
K																											
J																											
H																											
G																											
F																											
E																											
D																											
C																											
B																											
A																											

DRAWING INDEX	
SHEET NUMBER	DESCRIPTION
GENERAL	
G-001	COVER SHEET
G-002	DRAWING INDEX SHEET
CIVIL	
C-001	GENERAL INFORMATION SHEET
C-101	PLAN - GENERAL
C-102	PLAN - STA. 94+526 TO STA. 102+642
C-103	PLAN - STA. 102+642 TO STA. 113+400
C-104	PLAN - STA. 113+400 TO STA. 124+900
C-105	PLAN - STA. 124+900 TO STA. 135+402
C-106	PLAN - FAIRLESS TURNING BASIN
C-107	PLAN - FAIRLESS TURNING BASIN GEOMETRY
C-201	PROFILE - FAIRLESS TURNING BASIN
C-301	TYPICAL SECTIONS - CHANNEL (STA. 102+500 TO STA. 126+000)
C-302	CROSS SECTIONS - FAIRLESS TURNING BASIN
C-401	PLAN - MONEY ISLAND CELL B DMPF



DELAWARE RIVER
PHILADELPHIA, PENNSYLVANIA TO TRENTON, NEW JERSEY
MAINTENANCE DREDGING
DRAWING INDEX SHEET




SHEET ID
G-002

DESIGNED BY: U.S. ARMY CORPS OF ENGINEERS
DRAWN BY: PHILADELPHIA DISTRICT
CHECKED BY: #
IN CHARGE: #
SUBMITTED BY: #
DATE: #


DESIGN SUBMITTAL DATE: #
SOLUTION NUMBER: #
PROJECT NUMBER: #
DRAWING NUMBER: #
PLOT DATE: #
FILE NAME: #
DWG. SIZE: #
PLOT NAME: #
PLOT DATE: #

DATE: #
DESCRIPTION: #

DRAWING SHEET SYMBOLS

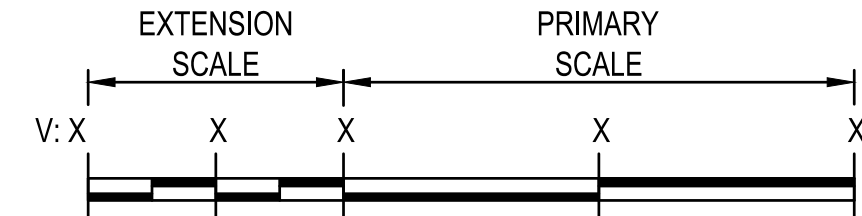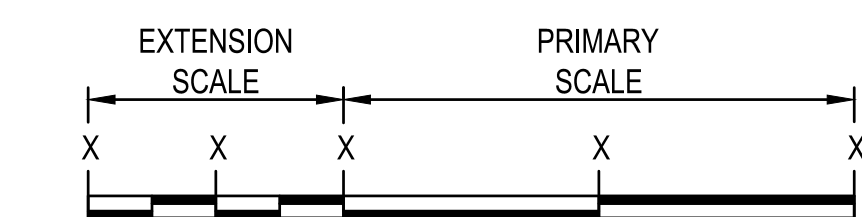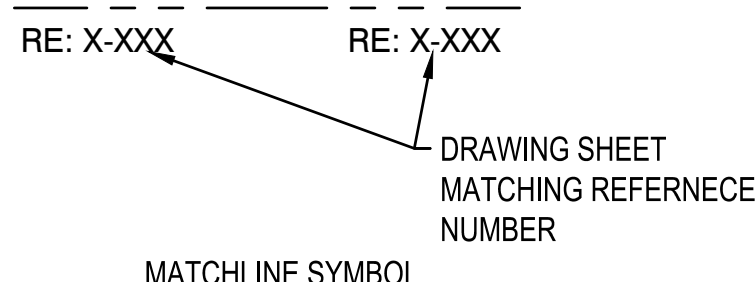

GRAPHIC BAR SCALE SYMBOLS

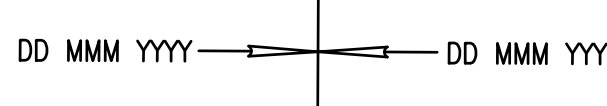

CHANNEL CENTERLINE

COORDINATE - NORTHING AND EASTING

ACCEPTANCE SECTION

BUOY MARKERS

APPROXIMATE LOCATION OF WORK

APPROXIMATE BORDERS OF GOVERNMENT
OWNED DISPOSAL AREAS TO BE USED IN
CONTRACT

REQUIRED DREDGING

ALLOWABLE OVERDEPTH

DATE OF SURVEYS

BOTTOM SAMPLE

VIRBACORE SAMPLE

GENERAL NOTES

1. THE EXISTING SITE CONDITION SURVEYS ARE A RESULT OF SURVEYS CONDUCTED IN OCTOBER 2024 (LEHIGH TO FLORENCE), MAY 2024 (FLORENCE TO NEVBOLD), FEBRUARY 2025 (FAIRLESS TURNING BASIN) AND DECEMBER 2024 (BLAKE TO DUCK ISLAND), AND CAN ONLY BE CONSIDERED REPRESENTATIVE OF THE CONDITIONS OCCURRING AT THAT TIME.
2. HORIZONTAL REFERENCE - NAD 83, NEW JERSEY STATE PLANE, ZONE 2900, US SURVEY FEET.
3. SOUNDINGS ARE EXPRESSED IN FEET AND TENTHS AND REFER TO MEAN LOWER LOW WATER (MLLW). SEE DETAILS ON THIS SHEET FOR THE TIDAL REFERENCE FROM NOAA'S TIDAL EPOCH - 1983-2001.
4. CHANNEL SOUNDINGS WERE SELECTED FOR PLOTTING PURPOSES ONLY USING THE MINIMUM DEPTH WITHIN A 30'X30' CELL AND SHIFTED TO THE CELL'S CENTER. FAIRLESS TURNING BASIN SOUNDINGS WERE SELECTED FOR PLOTTING PURPOSES ONLY USING THE MINIMUM DEPTH WITHIN A 30'X30' CELL AND SHIFTED TO THE CELL'S CENTER. HYPACK MATRIX PROGRAM WAS USED TO PERFORM THE SOUNDING SELECTION.
5. DUE TO VARIATIONS IN RESOLUTION BETWEEN COLOR BANDS AND CONTOURS, SOME MINOR DISCREPANCIES MAY BE NOTED. COLOR BANDS ARE FOR PLOTTING PURPOSES ONLY. COLOR BANDS WERE GENERATED USING THE MINIMUM DEPTH WITHIN A 30'X30' CELL, AND SHIFTING TO THE CELL'S CENTER. HYPACK MATRIX PROGRAM WAS USED TO PERFORM THE SOUNDING SELECTION.
6. THIS SURVEY MEETS STANDARDS AS OUTLINED IN CORPS OF ENGINEERS HYDROGRAPHIC SURVEY MANUAL EM1110-2-1003, FOR NAVIGATION AND DREDGING SUPPORT SURVEYS.
7. QUESTIONS CONCERNING BOTH HORIZONTAL AND VERTICAL CONTROL SHOULD BE DIRECTED TO PHILADELPHIA DISTRICT CORPS OF ENGINEERS SURVEY BRANCH POB. STEPHEN FARRELL, AT (215) 656-6780.
8. THE POSITIONS OF THE AIDS TO NAVIGATION ARE PROVIDED FOR INFORMATION ONLY, AND SHOULD NOT BE USED FOR NAVIGATION.
9. FOR CHANNEL CENTERLINE GEOMETRY, SEE THE CONTRACT SPECIFICATIONS.
10. THE CONTRACTOR MUST COORDINATE WITH ALL APPROPRIATE UTILITY COMPANIES AND THE USACE RESIDENT OFFICE FOR MARK-OUT OF ONSITE UTILITIES PRIOR TO BEGINNING CONSTRUCTION ACTIVITIES.
11. SEE SPECIFICATIONS FOR DATUM CONVERSION INFORMATION.

GENERAL NOTES - DREDGED MATERIAL PLACEMENT FACILITY:

1. THE GOVERNMENT FURNISHED DREDGED MATERIAL PLACEMENT FACILITY (DMPF) AVAILABLE FOR USE UNDER THIS CONTRACT IS MONEY ISLAND CELL B. SEE SHEET C-401 FOR DMPF PLANS.
2. THE END OF ALL DISCHARGE PIPES SHALL BE LOCATED INSIDE THE DISPOSAL AREA LIMITS AS SPECIFIED IN THE CONTRACT SPECIFICATIONS. PIPE SHALL BE LOCATED SUCH THAT THE DISCHARGE DOES NOT EXPOSE FACE OR THE TOE-OF-SLOPE OF THE DISPOSAL AREA DIKE IN THE VICINITY OF THE DISCHARGE AREA.
3. BORROW FOR DIKING MATERIAL MAY BE OBTAINED FROM WITHIN THE DISPOSAL AREAS, BUT NOT CLOSER THAN 50 FEET FROM THE INSIDE TOE OF THE DIKE SECTIONS.
4. SHOULD THE CONTRACTOR DESIRE TO MODIFY THE DISCHARGE LIMITS SHOWN, APPROVAL MUST BE GRANTED BY THE CONTRACTING OFFICER PRIOR TO MODIFICATION.
5. TOPOGRAPHY SHOWN WAS GENERATED USING PHOTOGRAMMETRIC METHODS BASED ON AERIAL PHOTOGRAPHY DATED DECEMBER 19, 2018. A TOP OF DIKE SURVEY DATED 27 OCTOBER 2023 WAS PREPARED USING INDIVIDUAL GPS SHOTS ON SITE. CONTOURS (2 FOOT INTERVAL) AND SPOT ELEVATIONS SHOWN CAN ONLY BE CONSIDERED REPRESENTATIVE OF THE SITE CONDITIONS AS THEY EXISTED AT THE DATES INDICATED. EARTHWORK ACTIVITIES HAVE TAKEN PLACE SINCE THE TOPOGRAPHY WAS GENERATED. CONTRACTORS ARE STRONGLY ENCOURAGED TO VISIT THE SITE WHERE WORK IS TO BE PERFORMED TO ACQUAINT THEMSELVES WITH EXISTING CONDITIONS THAT COULD AFFECT THE PROJECT COST.
6. MAPPING WAS COMPILED BY USING (AEROMETRIC) PHOTOGRAMMETRIC METHODS FROM AERIAL PHOTOGRAPHY DATED JANUARY 9, 2014. THIS MAPPING WAS COMPILED IN ACCORDANCE WITH THE NATIONAL STANDARD FOR SPATIAL DATA ACCURACY (NSSDA) ACCURACY STANDARDS FOR MAPS AT 1 INCH=62500 200 FT. SCALE.
7. THE SITE IS GENERALLY CLEAR WITH PASSABLE ACCESS ROADS, BUT SOME MINOR CLEARING OF VEGETATION MAY BE REQUIRED IN ISOLATED LOCATIONS TO GAIN ACCESS.
8. HORIZONTAL REFERENCE - NAD 83, NEW JERSEY STATE PLANE, ZONE 2900, US SURVEY FEET.
9. THE VERTICAL REFERENCE FOR MONEY ISLAND DREDGED MATERIAL PLACEMENT FACILITY IS MSL WHICH IS 0.48 ABOVE NAVD88.

ABBREVIATIONS

ABBREVIATIONS					
ABBRV	DESCRIPTION	ABBRV	DESCRIPTION	ABBRV	DESCRIPTION
AD	AREA DRAIN	EXT	EXTERIOR	PIV	POST INDICATOR VALVE
ADDL	ADDITIONAL	FDN	FOUNDATION	PSF	POUNDS PER SQUARE FOOT
BC	BOTTOM OF CURB	FF	FINISHED FLOOR	PSI	POUNDS PER SQUARE INCH
BD	BOARD	FFE	FINISHED FLOOR ELEVATION	PT	POINT OF TANGENCY
BIT	BITUMINOUS	FIN	FINISH	PVC	POLYVINYL CHLORIDE
BL or	BASE LINE	FL	FLOOR	PVI	POINT OF VERTICAL INFLECTION
BLDG	BUILDING	FM	FORCE MAIN	R, RAD	RADIUS
BMP	BEST MANAGEMENT PRACTICE	FT	FOOT, FEET	REINF	REINFORCEMENT
BOT	BOTTOM	FTG	FOOTING	ROW	RIGHT OF WAY
BW	BOTTOM OF WALL	G	GROUND	RT	RIGHT
BVCE	BEGINNING OF VERTICAL CURVE ELEVATION	GOVT	GOVERNMENT	S	SOUTH
BVCS	BEGINNING OF VERTICAL CURVE STATION	GR	GRADE	SCH	SCH
CB	CATCH BASIN	HDPE	HIGH DENSITY POLYETHYLENE	SECT	SECTION
CC or C-C	CENTER TO CENTER	HORIZ	HORIZONTAL	SF	SQUARE FEET, SILT FENCE
CL or	CENTERLINE	HP	HIGH POINT	SPEC	SPECIFICATION
CMP	CONCRUGATED METAL PIPE	HS	HIGH STRENGTH	SO	SOUND
CMU	CONCRETE MASONRY UNIT	HT	HEIGHT	SST	STAINLESS STEEL
CD	CLEAN OUT	ID	INSIDE DIAMETER	STA	STATION
COL	COLUMN	INCH		STRU or STRUC	STRUCTURE, STRUCTURAL
CONC	CONCRETE	INSUL	INSULATION, INSULATED	SUSP	SUSPENDED
CONSTR	CONSTRUCTION	INT	INTERIOR	TEMP	TEMPORARY
CONT	CONTINUOUS	INV	INVERT	TC	TOP OF CURB
COR	CONTRACTING OFFICER'S REPRESENTATIVE	LL	LIVE LOAD	TD	TRENCH DRAIN
CTRL	CONTROL	LP	LOW POINT	TDO	TRENCH DRAIN OUTLET
CWL	CONTRACTOR WORK LIMIT	LT	LEFT, LIGHT	TELE	TELEPHONE
DGA	DENSE GRADED AGGREGATE	LVC	LENGTH OF VERTICAL CURVE	TG	TOP OF GRATE
DIA	DIAMETER	JCT	JUNCTION	TOPO	TOPOGRAPHY
DIM	DIMENSION	MATL	MATERIAL	TW	TOP OF WALL
DMPF	DREDGED MATERIAL PLACEMENT FACILITY	MAX	MAXIMUM	TYP	TYPICAL
DWG	DRAWING	MHW	MEAN HIGH WATER	UD	UNDERDRAIN
E	EAST	MIN	MINIMUM	UDO	UNDERDRAIN OUTLET PIPE
EA	EACH	MISC	MISCELLANEOUS	UE	UNDERGROUND ELECTRIC
ECM	EROSION CONTROL MAT	MLLW	MEAN LOWER LOW WATER	UGND	UNDERGROUND
EL or ELEV	ELEVATION	NLW	MEAN LOW WATER	UOP	UNDERDRAIN OUTLET PIPE
ELC	ELECTRIC	N	NORTH	UXO	UNEXPLODED ORDNANCE
ELL	ELLIPITICAL	NT	NOT LESS THAN	VC	VERTICAL CURVE
EOP	EDGE OF PAVEMENT	NTS	NOT TO SCALE	VOL	VOLUME
EOS	EDGE OF SHOULDER	OC	ON CENTER	VERT	VERTICAL
EQ	EQUAL, EQUALITY	OD	OUTSIDE DIAMETER	W	WITH
EQUIP	EQUIPMENT	OH	OVERHEAD	WI	WEST
EW or E-W	EACH WAY	OPP	OPPOSITE	WL	WATER LEVEL
EXIST or EX	EXISTING	PC	POINT OF CURVE	WS	WATER SURFACE
EXP	EXPANSION, EXPOSED	PD	PAVEMENT DRAIN	WSEL	WATER SURFACE ELEVATION
EXP JT	EXPANSION JOINT	PI	POINT OF INFLECTION	W/O	WITHOUT


[illegible]

U.S. ARMY CORPS OF ENGINEERS PHILADELPHIA DISTRICT	DESIGNED BY: L. MULHILL	ISSUE/SUBMITAL DATE: JUNE 2025
	DRAWN BY: L. MULHILL	SOLICITATION NUMBER: W9726295003
	CHECKED BY:	CONTRACT NUMBER:
#	SO. DRAWN BY: L. MULHILL	PLOT DATE: 9 JUNE 2025
#	SCALE: 1"=100'	
#	FILE NAME:	
#	DWS. SIZE:	
#	C-001 GENERAL INFORMATION SHEET.dwg	

DELAWARE RIVER
PHILADELPHIA, PENNSYLVANIA TO TRENTON, NEW JERSEY
MAINTENANCE DREDGING
GENERAL INFORMATION SHEET

SHEET ID



C-001

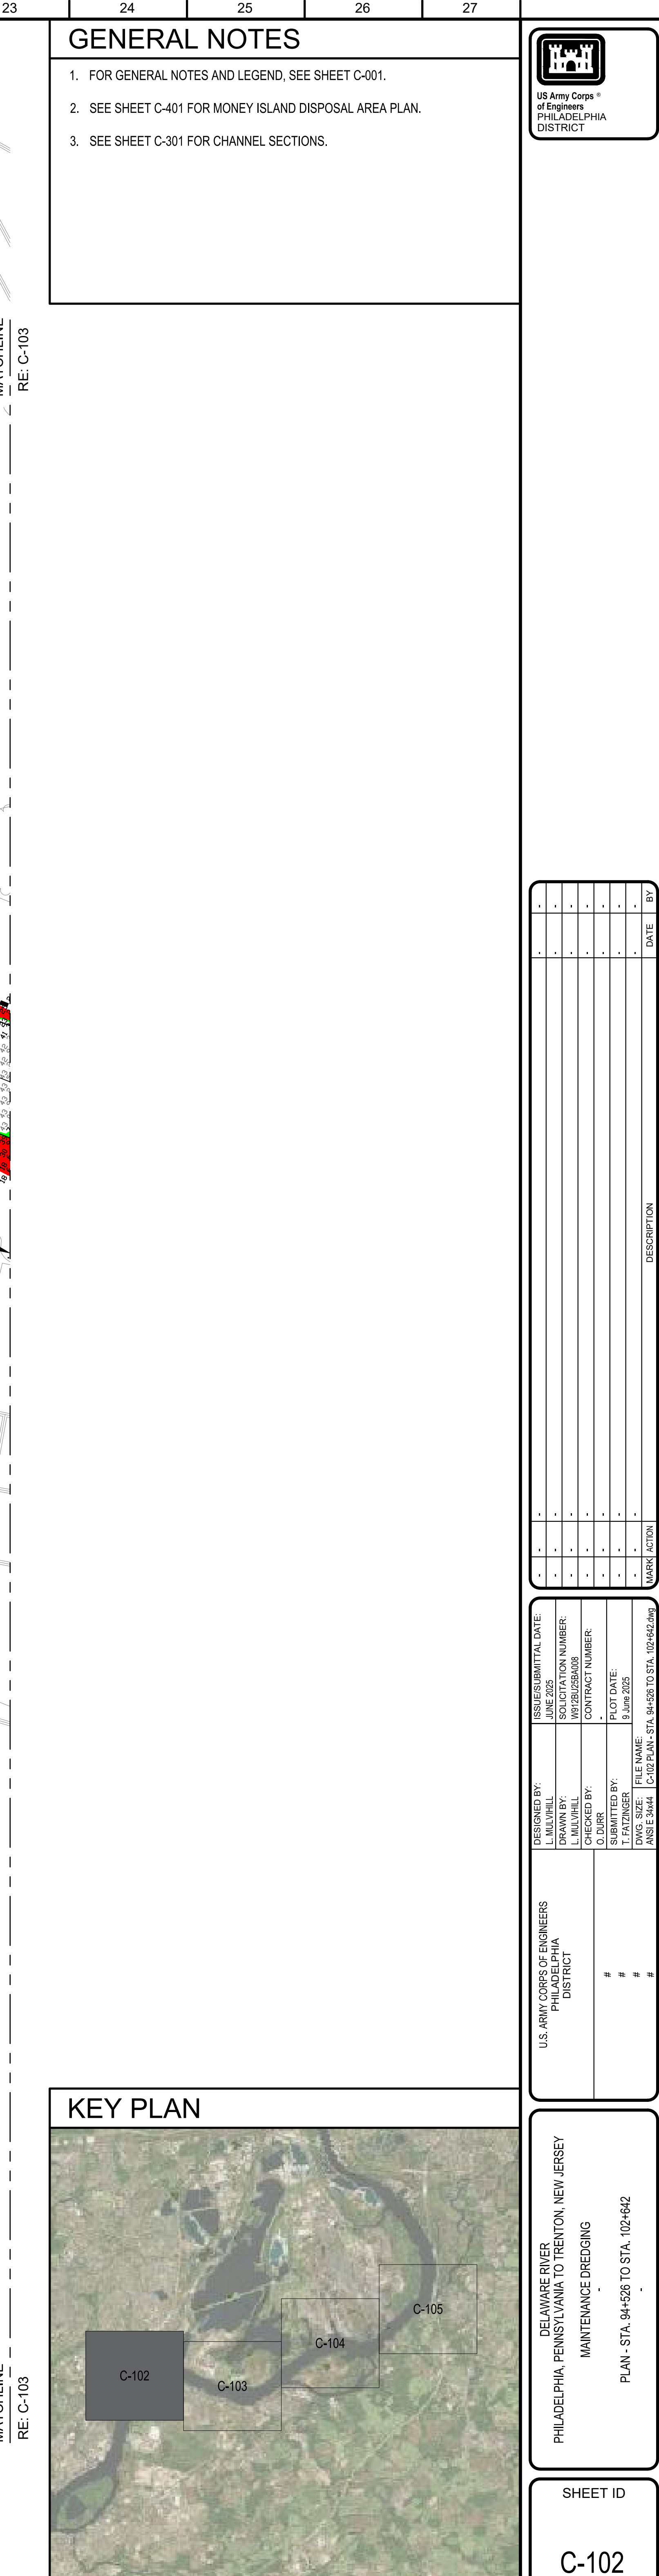[illegible]


U.S. ARMY CORPS OF ENGINEERS PHILADELPHIA DISTRICT		DESIGNED BY: M. W. MILL CHECKED BY: L. M. HALL	ISSUED/SUBMITTAL DATE: JUNE 2002
		CONTRACT NUMBER: W91B6U3BA009	CONTRACT NUMBER
		CHECKED BY: O. DURR	CONTRACT NUMBER
		SUBMITTED BY: T. FATZINGER	PLOT DATE: 9 June 2005
		DWG. SIZE: ANSI: A44	FILE NAME: C:\02 PLAN - STA. 102-462.dwg

DELAWARE RIVER
PHILADELPHIA, PENNSYLVANIA TO TRENTON, NEW JERSEY
MAINTENANCE DREDGING
PLAN - STA. 94+526 TO STA. 102+642

SHEET ID
C-102

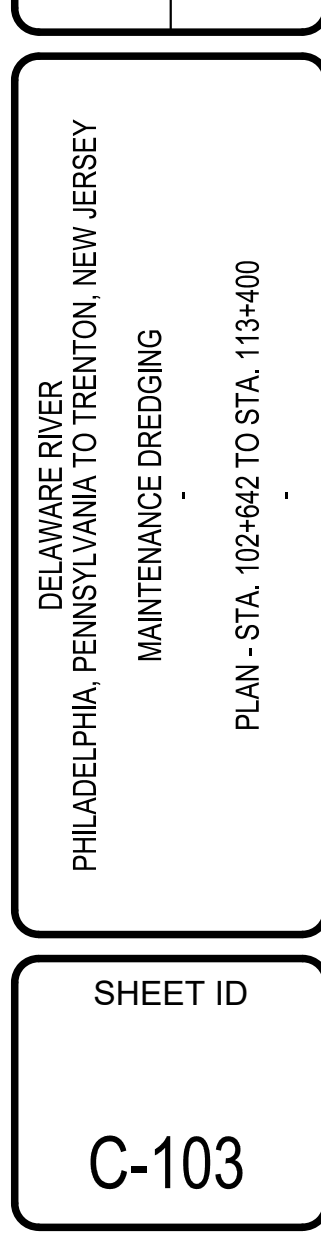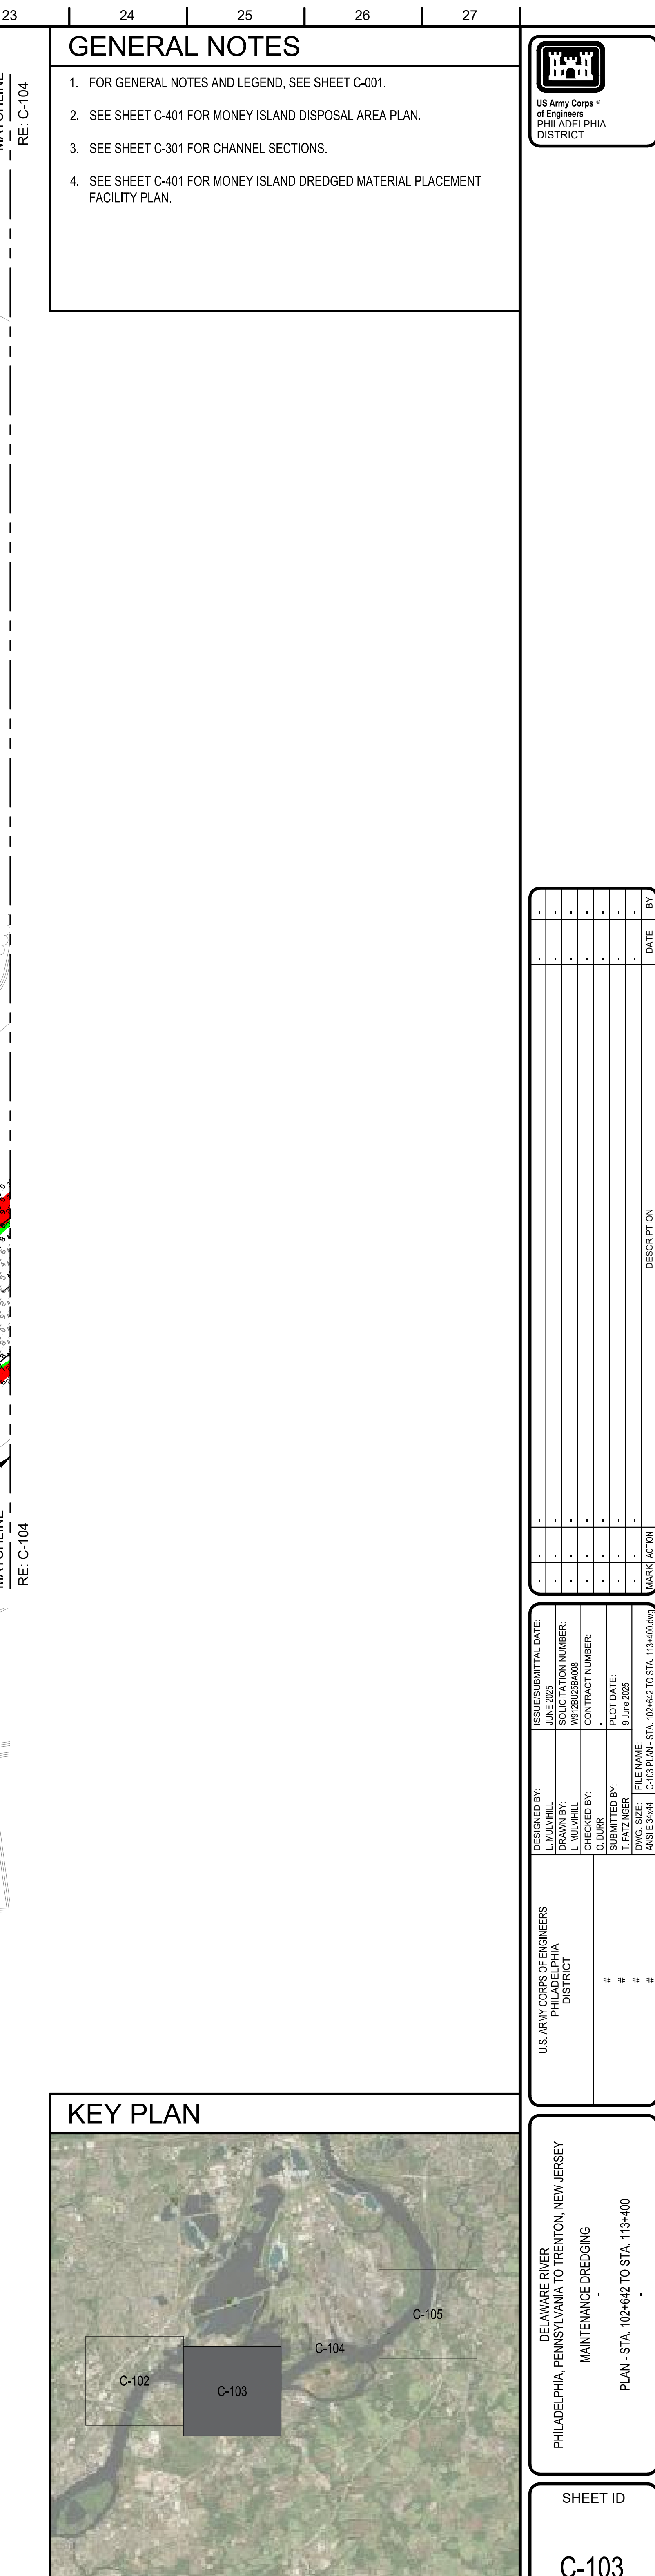

100% RTA

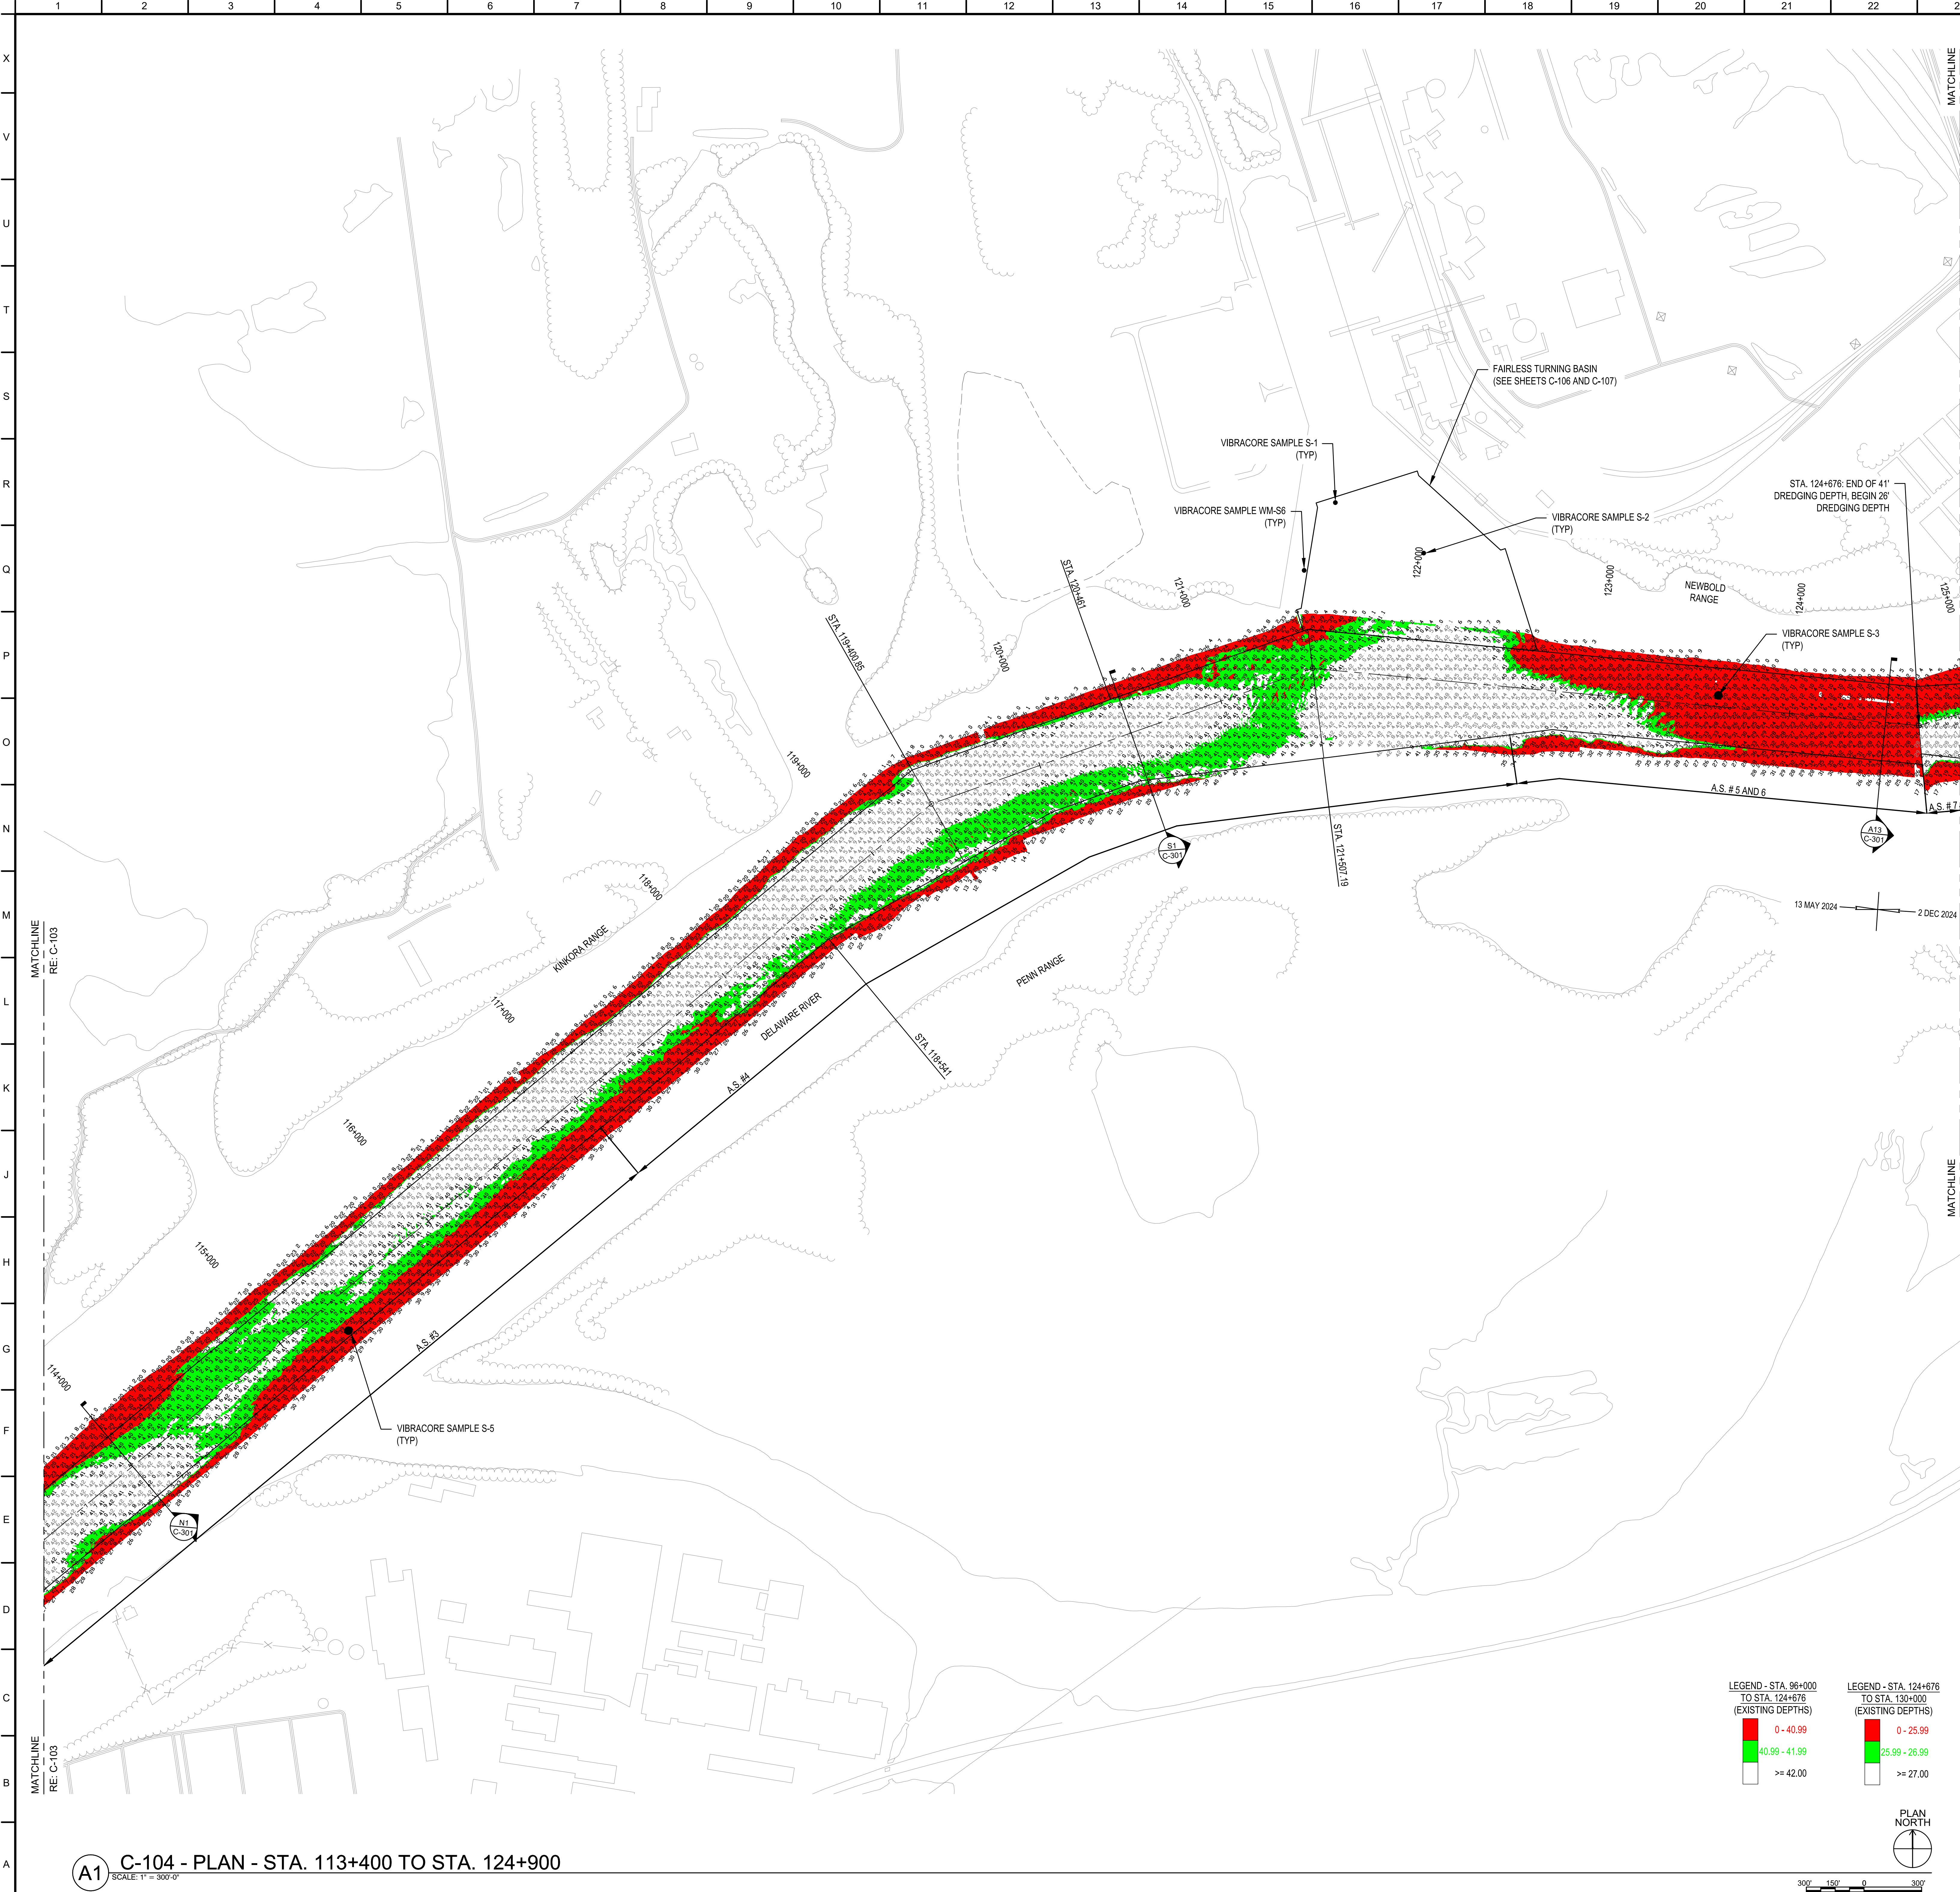

GENERAL NOTES

1. FOR GENERAL NOTES AND LEGEND, SEE SHEET C-001.
2. SEE SHEET C-401 FOR MONEY ISLAND DISPOSAL AREA PLAN.
3. SEE SHEET C-301 FOR CHANNEL SECTIONS AND SHEET C-302 FOR FAIRLESS TURNING BASIN SECTIONS.
4. SEE SHEET C-106 FOR FAIRLESS TURNING BASIN SURVEY AND SHEET C-107 FOR FAIRLESS TURNING BASIN GEOMETRY.



NO.	DATE	DESCRIPTION
1	13 MAY 2024	ISSUED FOR CONSTRUCTION
2	2 DEC 2024	ISSUED FOR CONSTRUCTION

DESIGNED BY: L. MULLEN	DESIGNER: L. MULLEN	DESIGNER: L. MULLEN
DRAWN BY: G. DUB	DRAWN BY: G. DUB	DRAWN BY: G. DUB
CHECKED BY: G. DUB	CHECKED BY: G. DUB	CHECKED BY: G. DUB
APPROVED BY: G. DUB	APPROVED BY: G. DUB	APPROVED BY: G. DUB
FILE NAME: C:\C-104\STA 113+400 TO STA 124+900.dwg	FILE NAME: C:\C-104\STA 113+400 TO STA 124+900.dwg	FILE NAME: C:\C-104\STA 113+400 TO STA 124+900.dwg
DATE: 13 MAY 2024	DATE: 13 MAY 2024	DATE: 13 MAY 2024

U.S. ARMY CORPS OF ENGINEERS PHILADELPHIA DISTRICT	DELAWARE RIVER PENNSYLVANIA TO TRENTON, NEW JERSEY MAINTENANCE DREDGING
---	---

SHEET ID C-104

KEY PLAN




A1 C-104 - PLAN - STA. 113+400 TO STA. 124+900



300' 150' 0' 300'

100% RFA

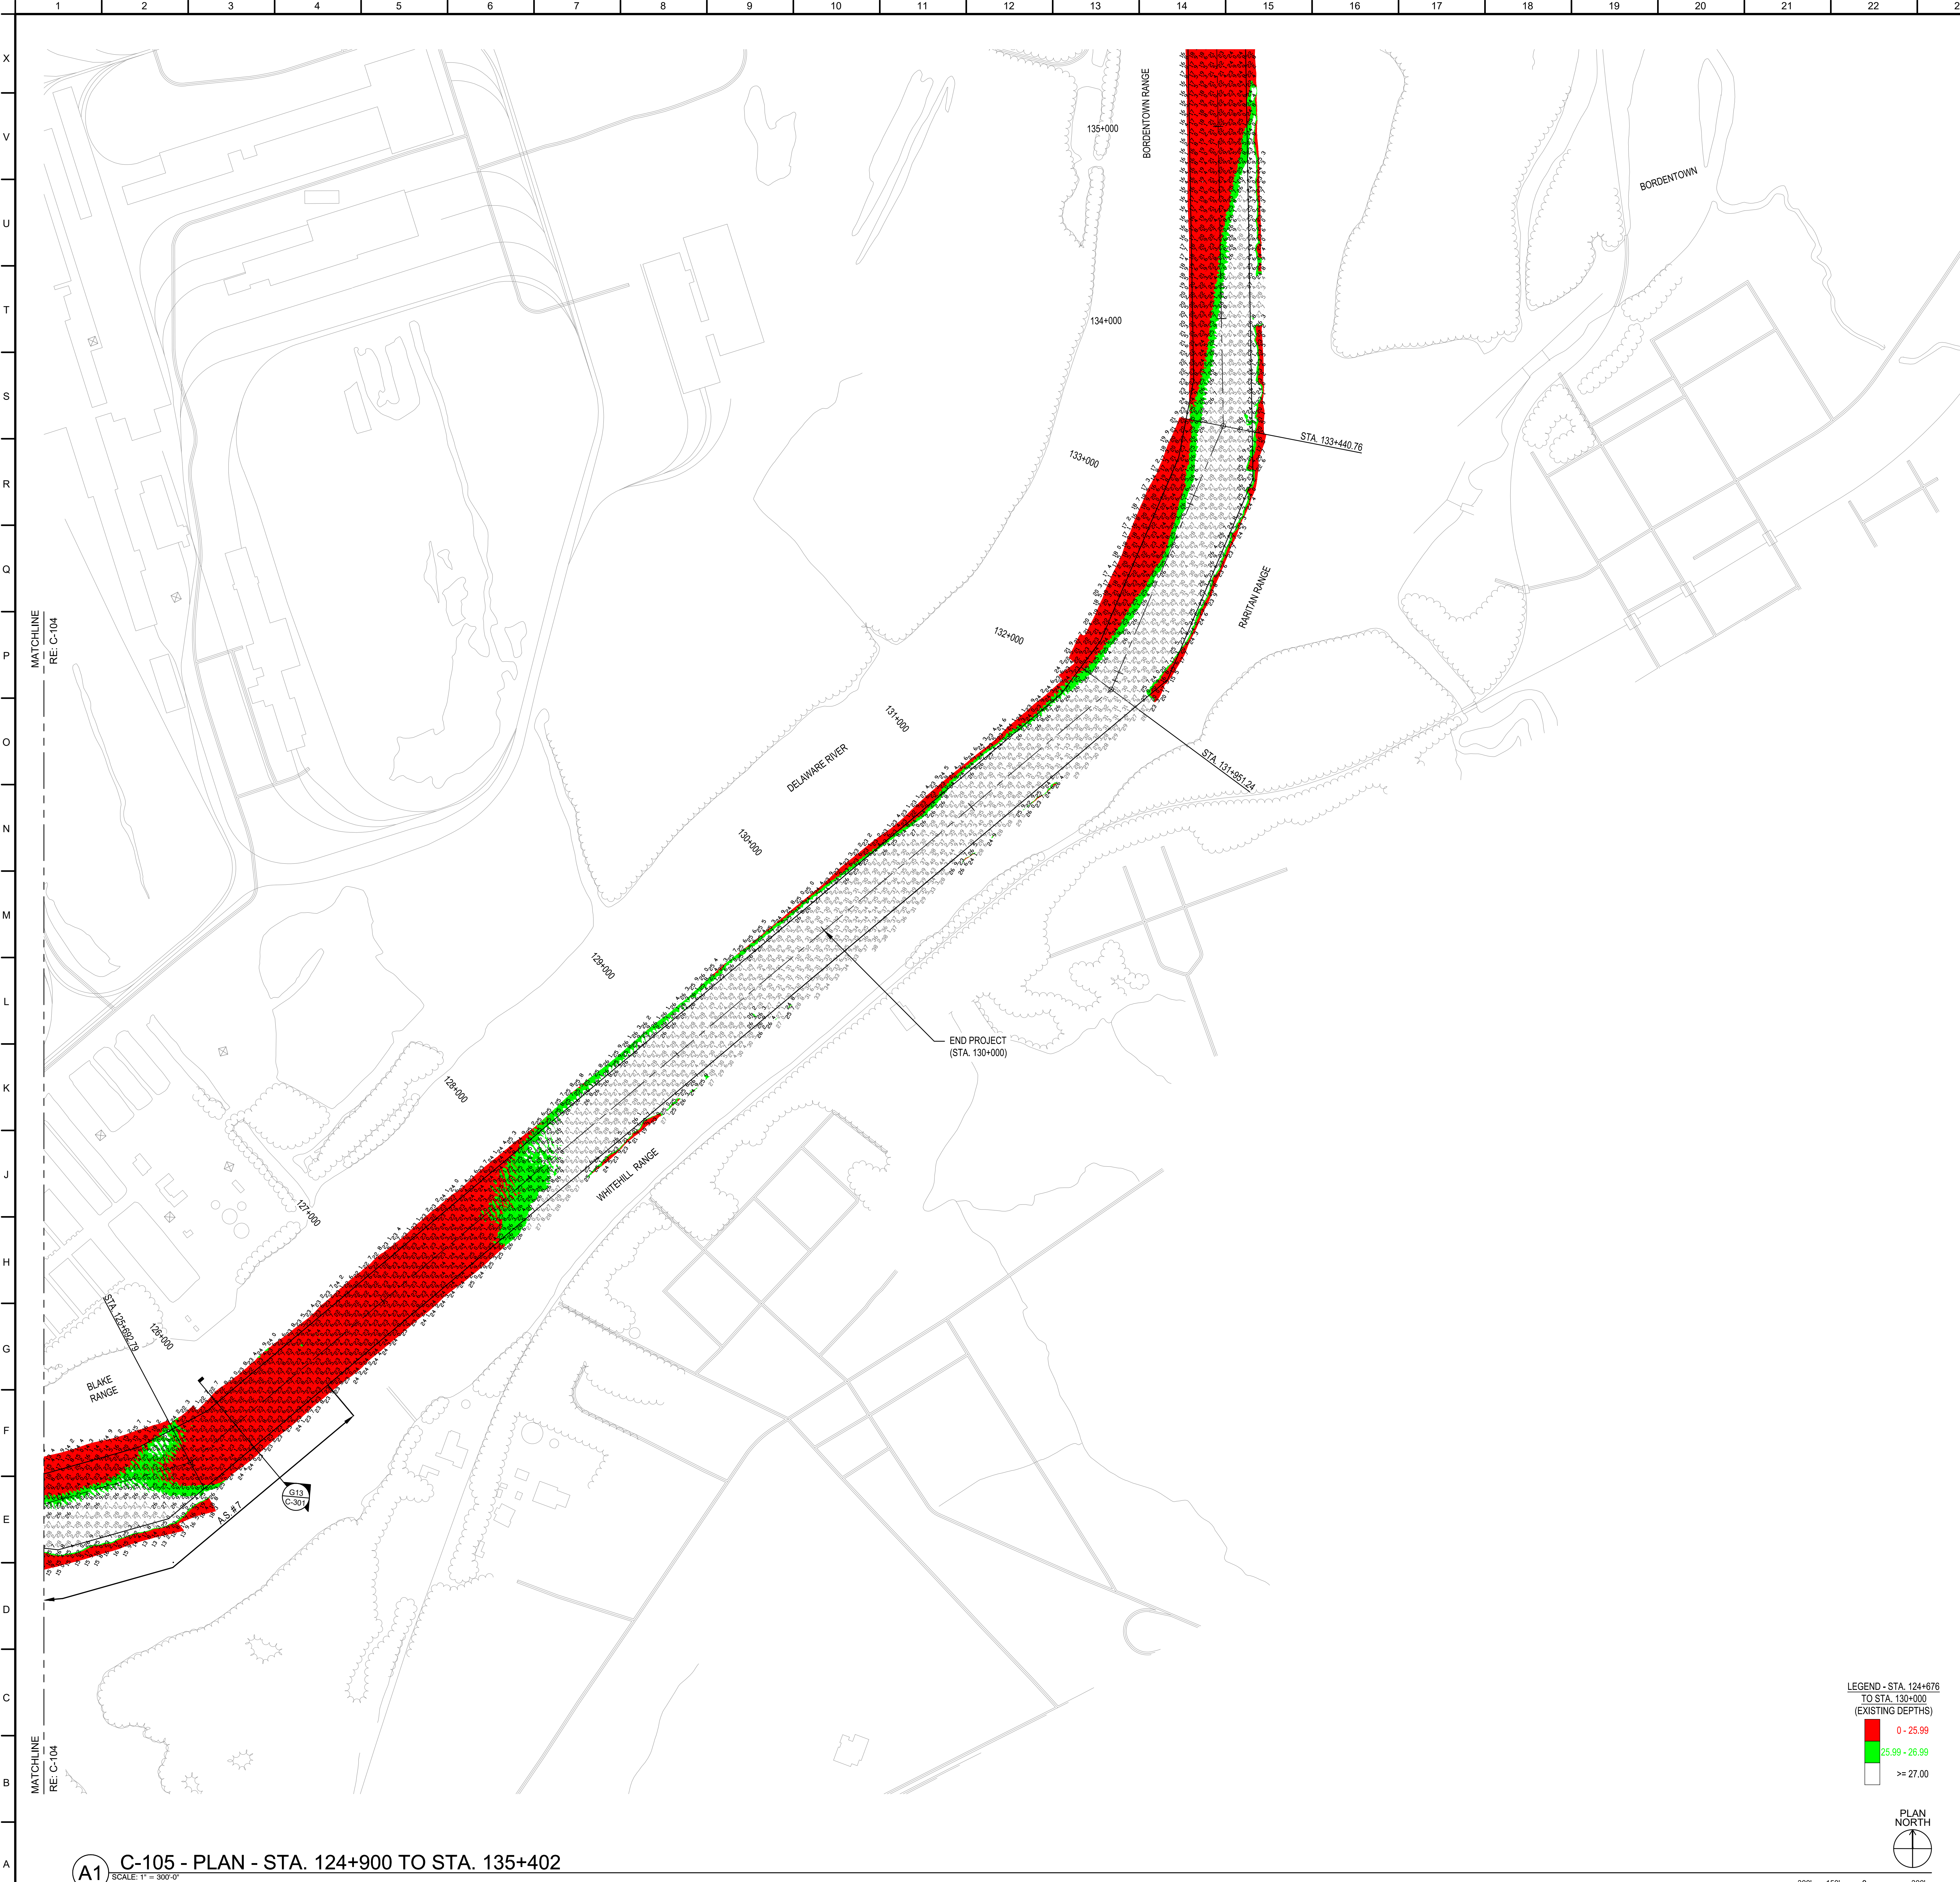

GENERAL NOTES

1. FOR GENERAL NOTES AND LEGEND, SEE SHEET C-001.
2. SEE SHEET C-401 FOR MONEY ISLAND DISPOSAL AREA PLAN.
3. SEE SHEET C-301 FOR CHANNEL SECTIONS.



DESIGNED BY:	DRAWN BY:	CHECKED BY:	IN CHARGE:	DATE:
U.S. ARMY CORPS OF ENGINEERS	U.S. ARMY CORPS OF ENGINEERS	U.S. ARMY CORPS OF ENGINEERS	U.S. ARMY CORPS OF ENGINEERS	U.S. ARMY CORPS OF ENGINEERS
PHILADELPHIA DISTRICT	PHILADELPHIA DISTRICT	PHILADELPHIA DISTRICT	PHILADELPHIA DISTRICT	PHILADELPHIA DISTRICT
PROJECT NUMBER:	PROJECT NUMBER:	PROJECT NUMBER:	PROJECT NUMBER:	PROJECT NUMBER:
FILE NAME:	FILE NAME:	FILE NAME:	FILE NAME:	FILE NAME:
DATE:	DATE:	DATE:	DATE:	DATE:

KEY PLAN



A1 C-105 - PLAN - STA. 124+900 TO STA. 135+402


LEGEND - STA. 124+676
TO STA. 130+000
(EXISTING DEPTHS)

0 - 25.99
25.99 - 26.99
>= 27.00



300' 150' 0' 300'

100% R/T

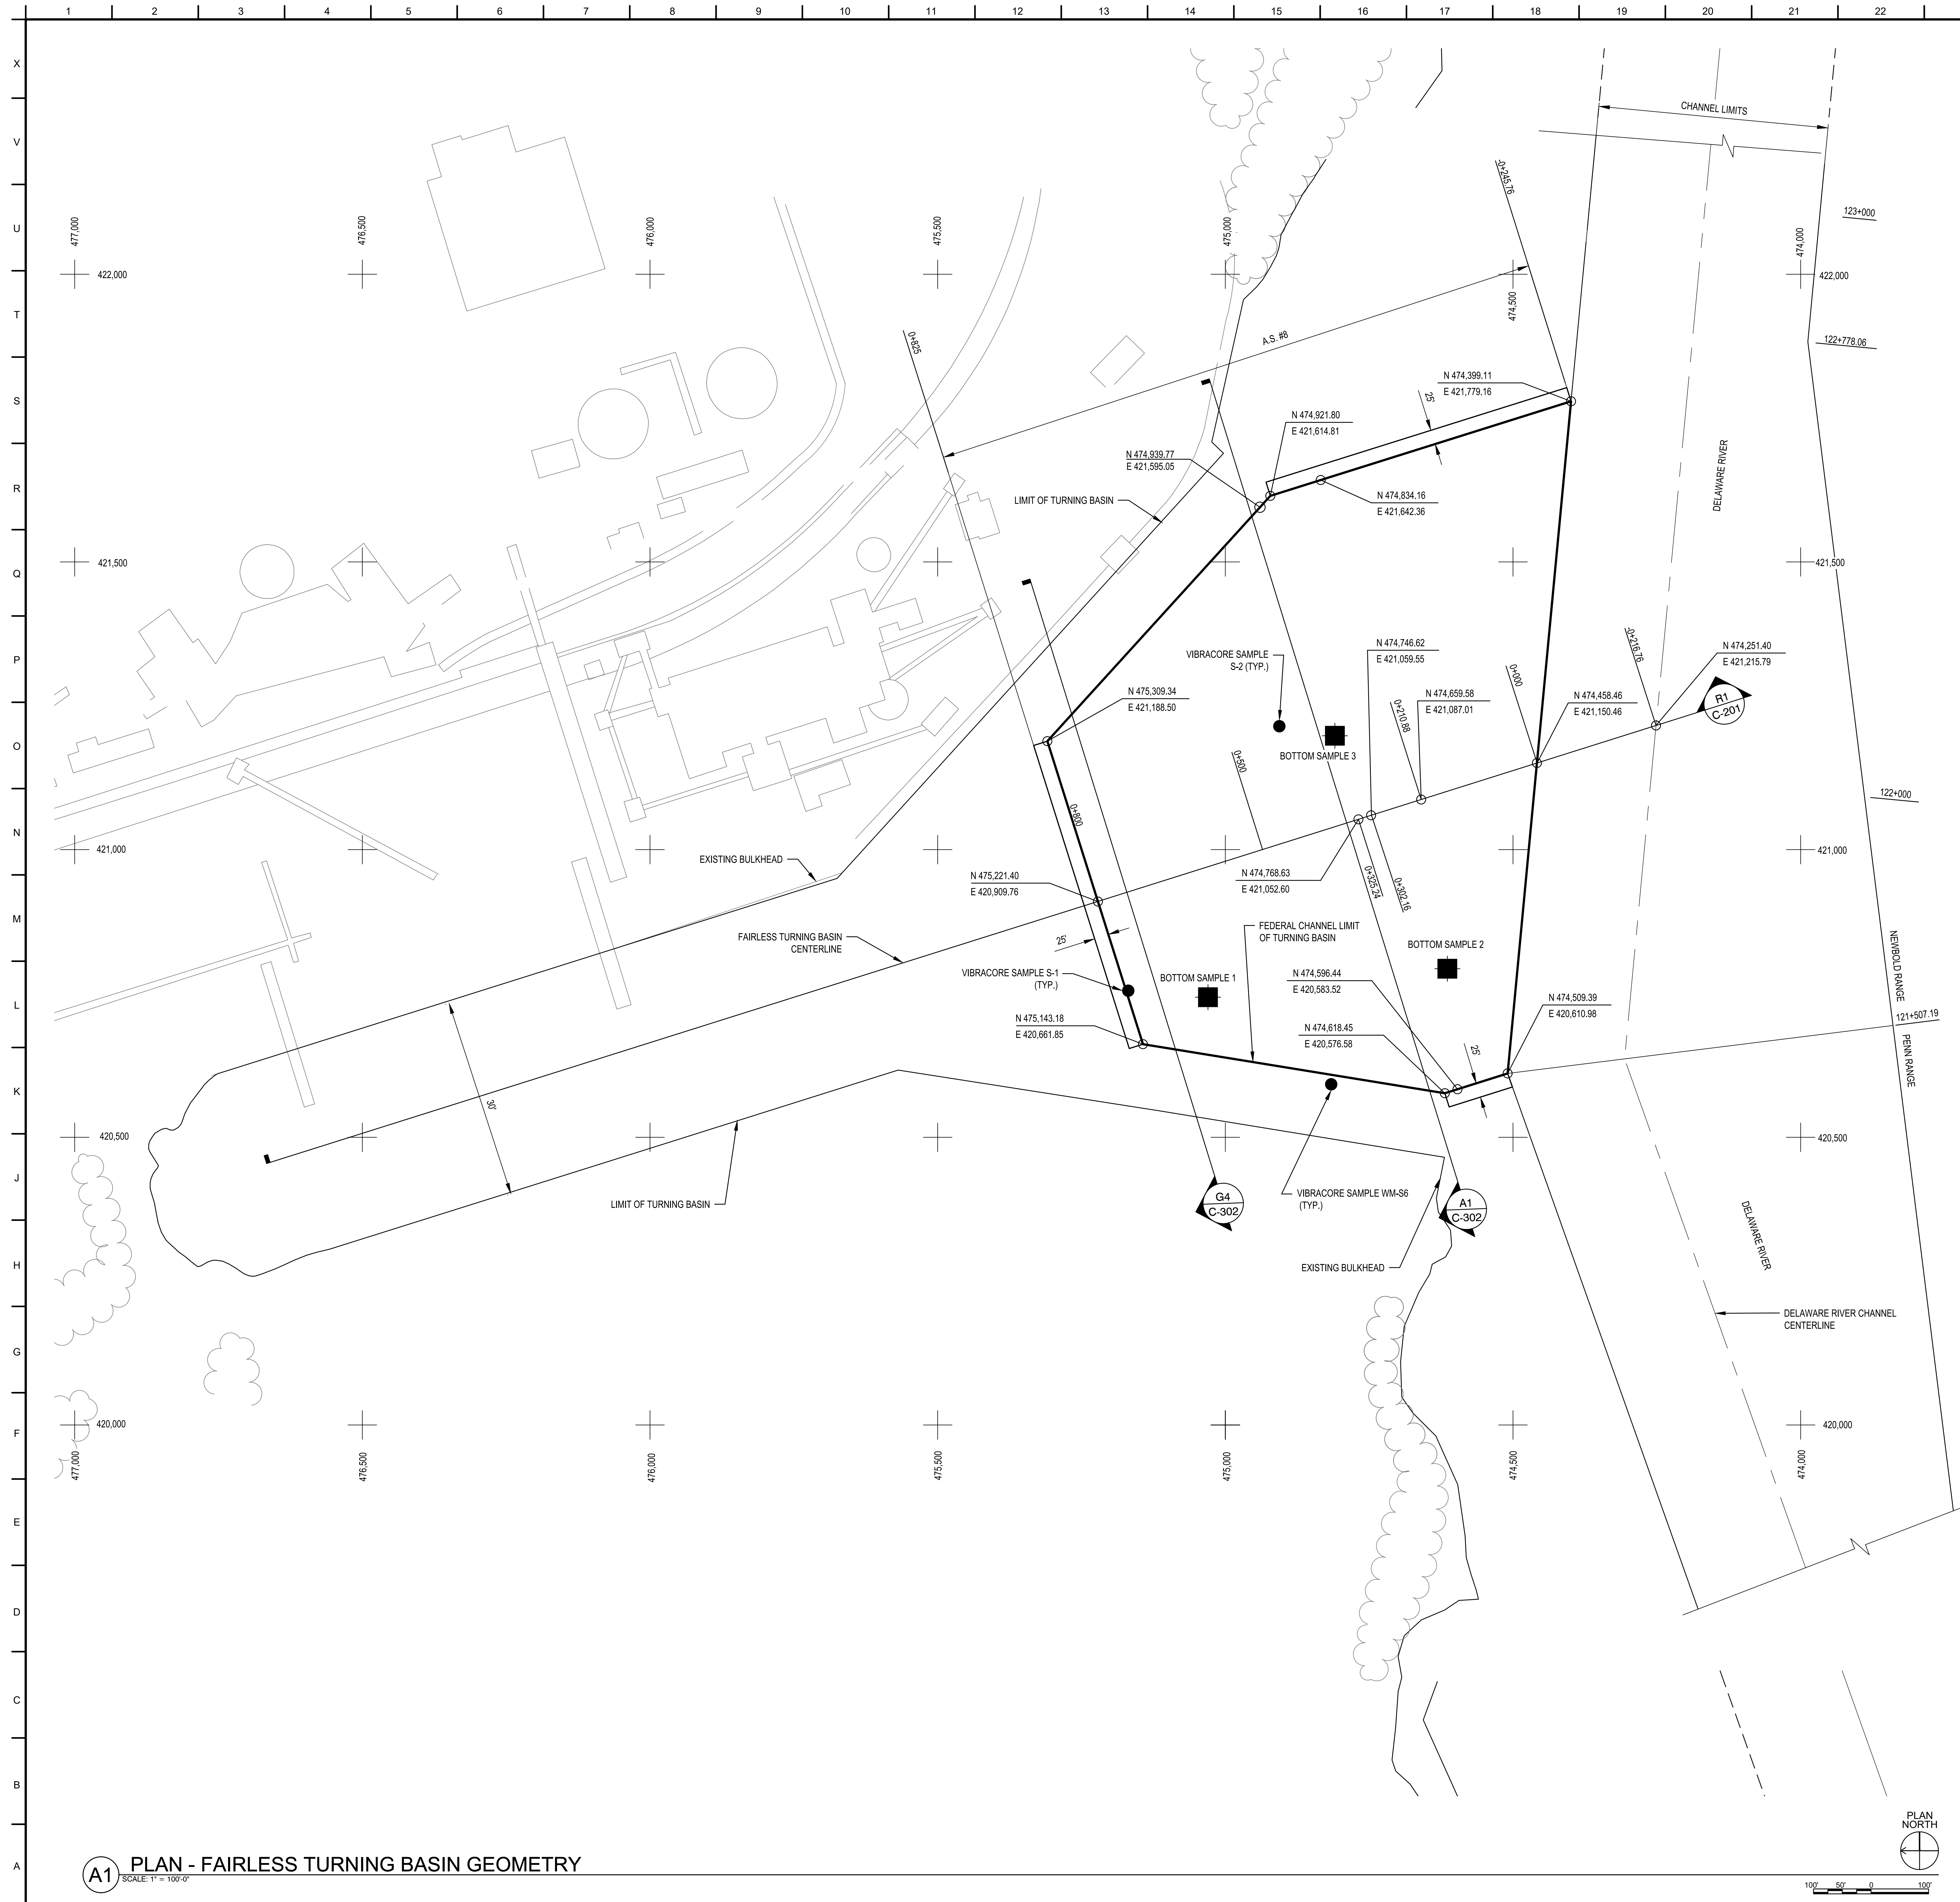

GENERAL NOTES

1. FOR GENERAL NOTES AND LEGEND, SEE SHEET C-001.
2. SEE SHEET C-401 FOR MONEY ISLAND DMPF PLAN.
3. SEE SHEET C-302 FOR FAIRLESS TURNING BASIN CROSS SECTIONS.



DATE	DESCRIPTION	AMOUNT	BY
1			
2			
U.S. ARMY CORPS OF ENGINEERS PHILADELPHIA DISTRICT	DESIGNED BY:	ISSUED/SUBMITTAL DATE:
	L. MULHILL	JUNE 1925
	DRAWN BY:	SOLICITATION NUMBER:
	L. MULHILL	W712U/2504/08
	CHECKED BY:	CONTRACT NUMBER:
	G. DUER	
	SUBMITTED BY:	PLOT DATE:
	T. FAZNER	JAN 1925
	FILE NAME:	
	ANSI 3444	CAD FILE NAME: 3-THIEN BASIN COWFITY.dwg


DELAWARE RIVER
PHILADELPHIA, PENNSYLVANIA TO TRENTON, NEW JERSEY
MAINTENANCE DREDGING
PLAN - FAIRLESS TURNING BASIN GEOMETRY

SHEET ID

C-107




1000

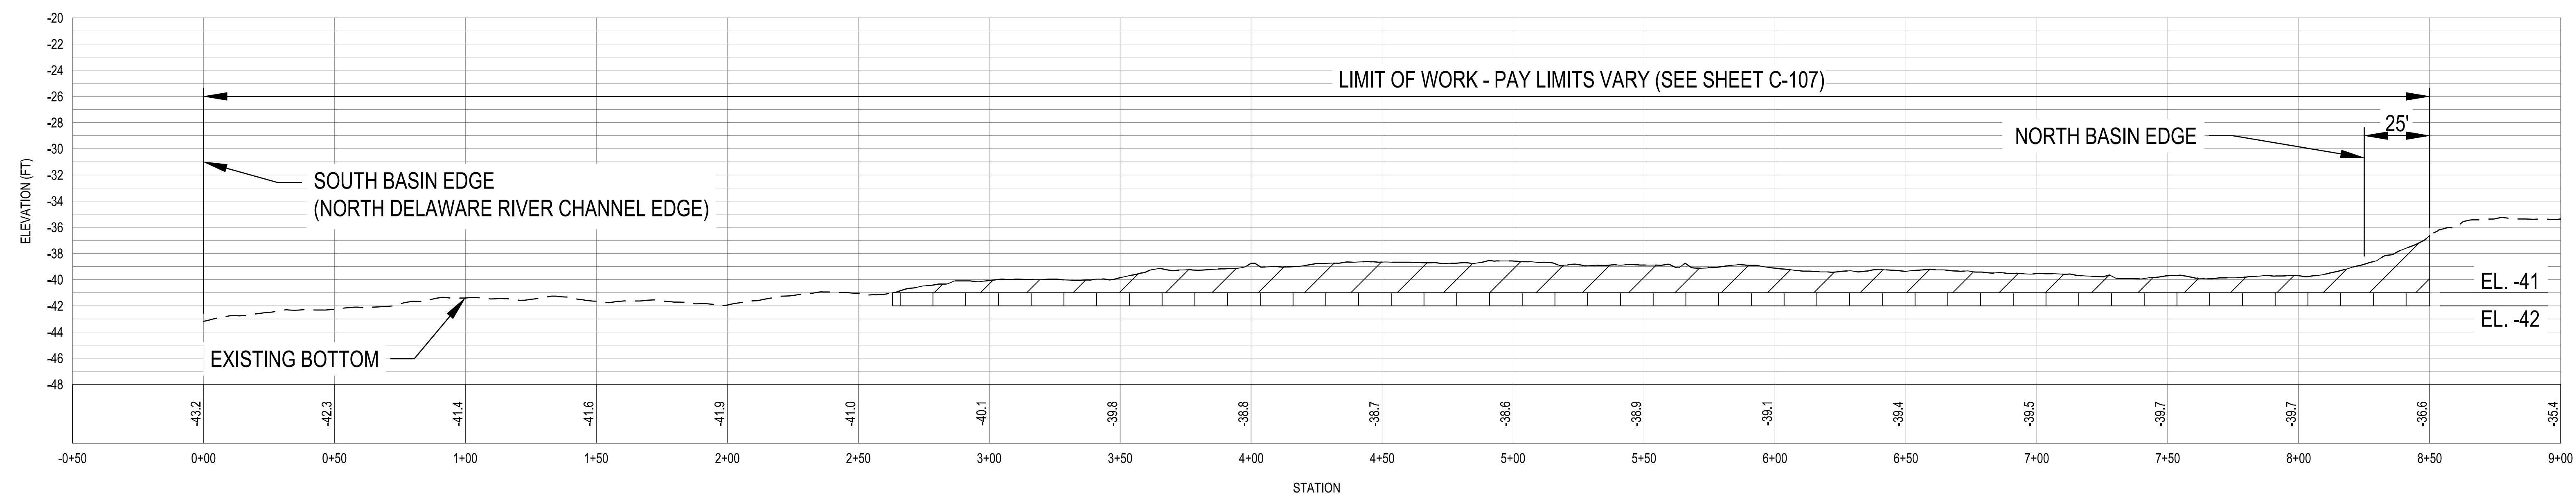


PROFILE - FAIRLESS TURNING BASIN CENTERLINE

SCALE IN FEET

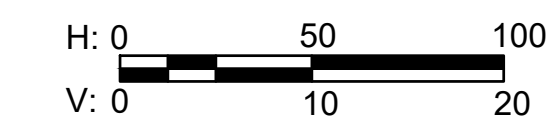

GENERAL NOTES

1. FOR GENERAL NOTES AND LEGEND, SEE SHEET C-001.
2. SEE SHEETS C-106 AND C-107 FOR FAIRLESS TURNING BASIN GEOMETRY AND SURVEY DATA.
3. SEE SHEET C-302 FOR FAIRLESS TURNING BASIN CROSS SECTIONS.

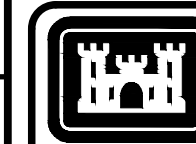

US Army Corps
of Engineers
PHILADELPHIA
DISTRICT

[illegible]

U.S. ARMY CORPS OF ENGINEERS PHILADELPHIA DISTRICT	DESIGNED BY:	J. MULVHILL	ISSUE/SUBMITTAL DATE:	JUNE 2025
	DRAWN BY:	J. MULVHILL	SOLICITATION NUMBER:	WY18DUS9A078
	CHECKED BY:	O. DURR	CONTRACT NUMBER:	
	SUBMITTED BY:	F. PACINER	PLOT DATE:	9 JUN 2025
	FILE NAME:	CONSE 3644		
	CDI PROJECT FUNDING TRAILING BASIN AND			

DELAWARE RIVER
PHILADELPHIA, PENNSYLVANIA TO TRENTON, NEW JERSEY
MAINTENANCE DREDGING
PROFILE - FAIRLESS TURNING BASIN



SHEET ID

C-201



100% BTA

GENERAL NOTES


1. FOR GENERAL NOTES AND LEGEND, SEE SHEET C-001.
2. SEE SHEETS C-106 AND C-107 FOR FAIRLESS TURNING BASIN GEOMETRY AND SURVEY DATA.

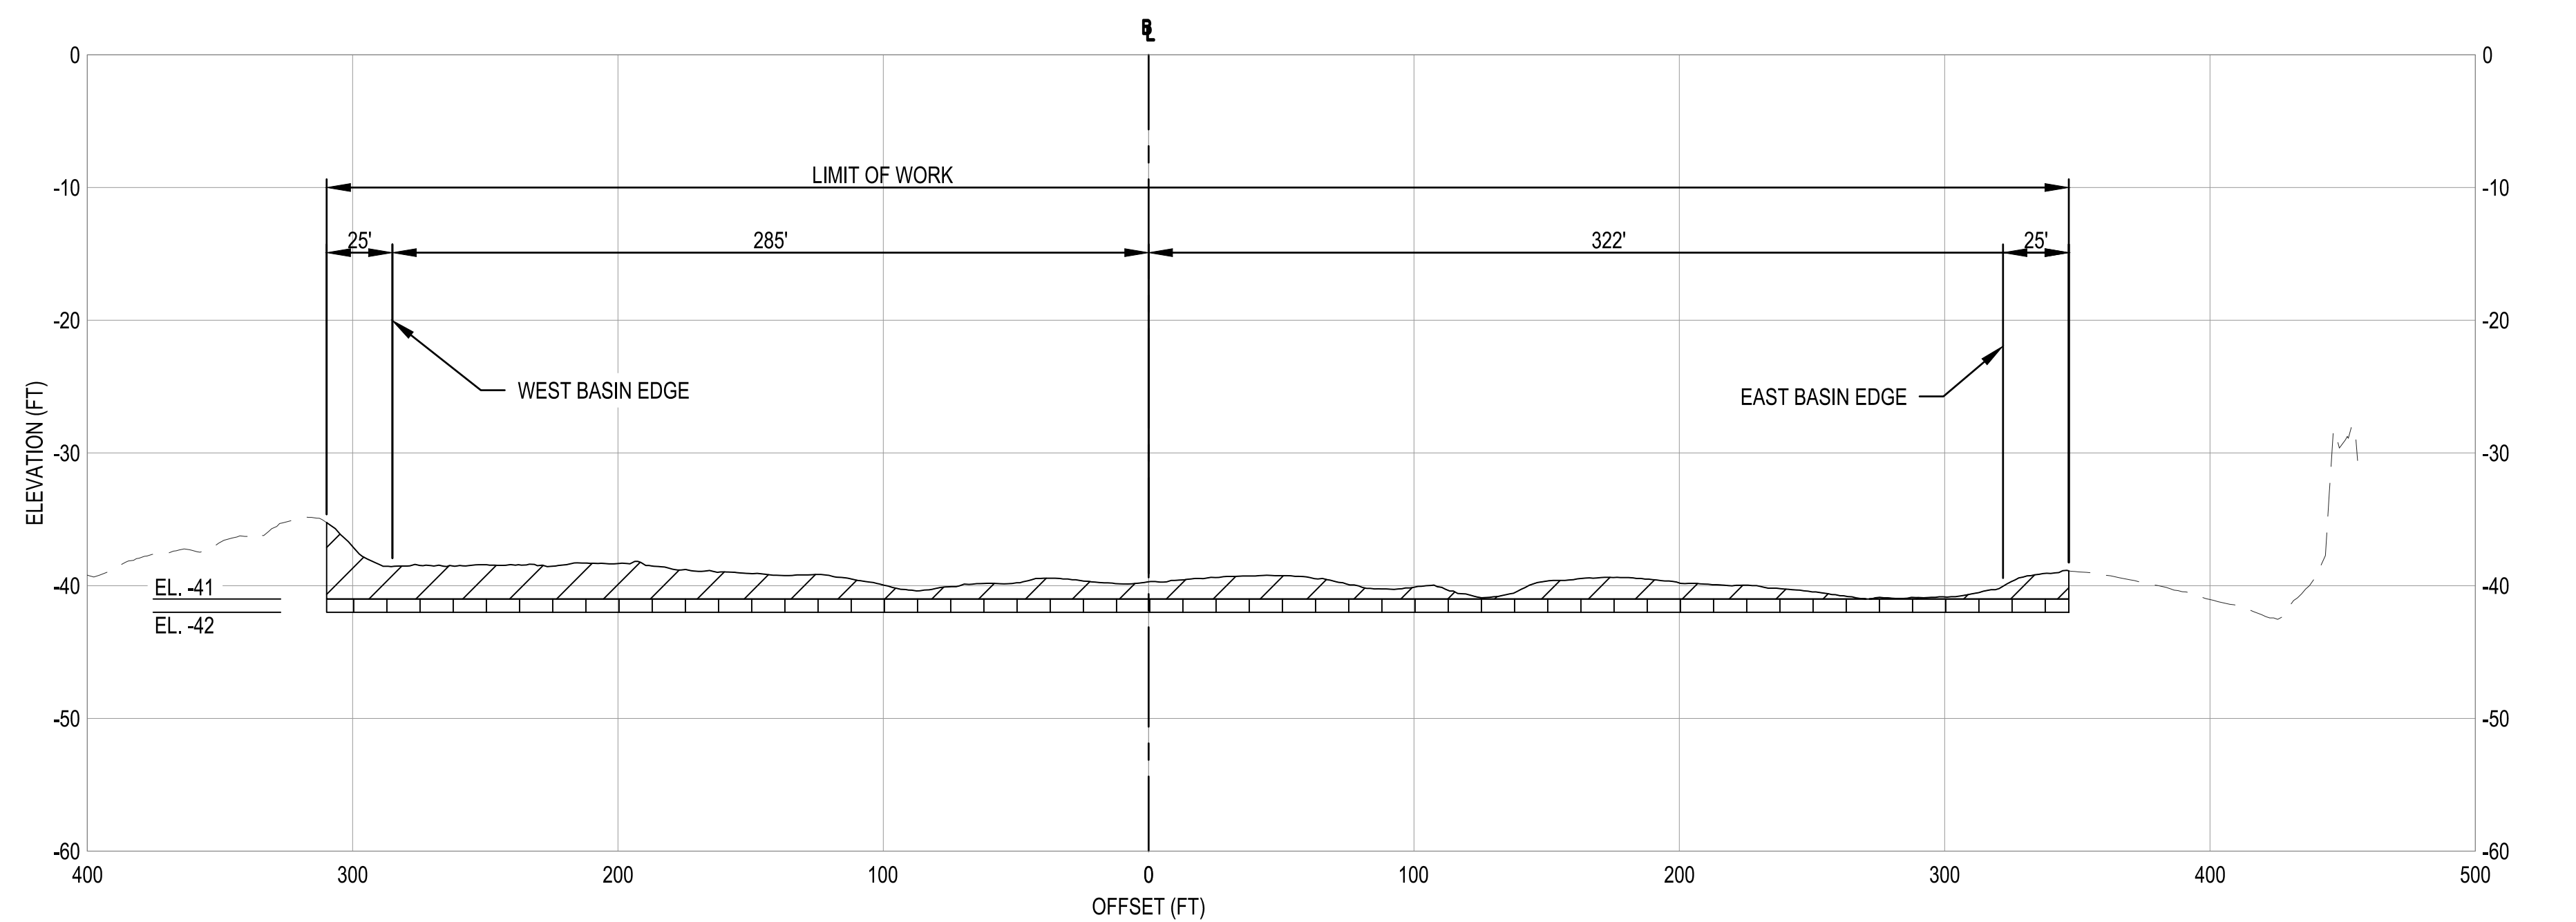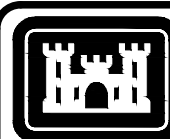

G4 CROSS SECTION - FAIRLESS TURNING BASIN (STA. 0+750)
SCALE IN FEET

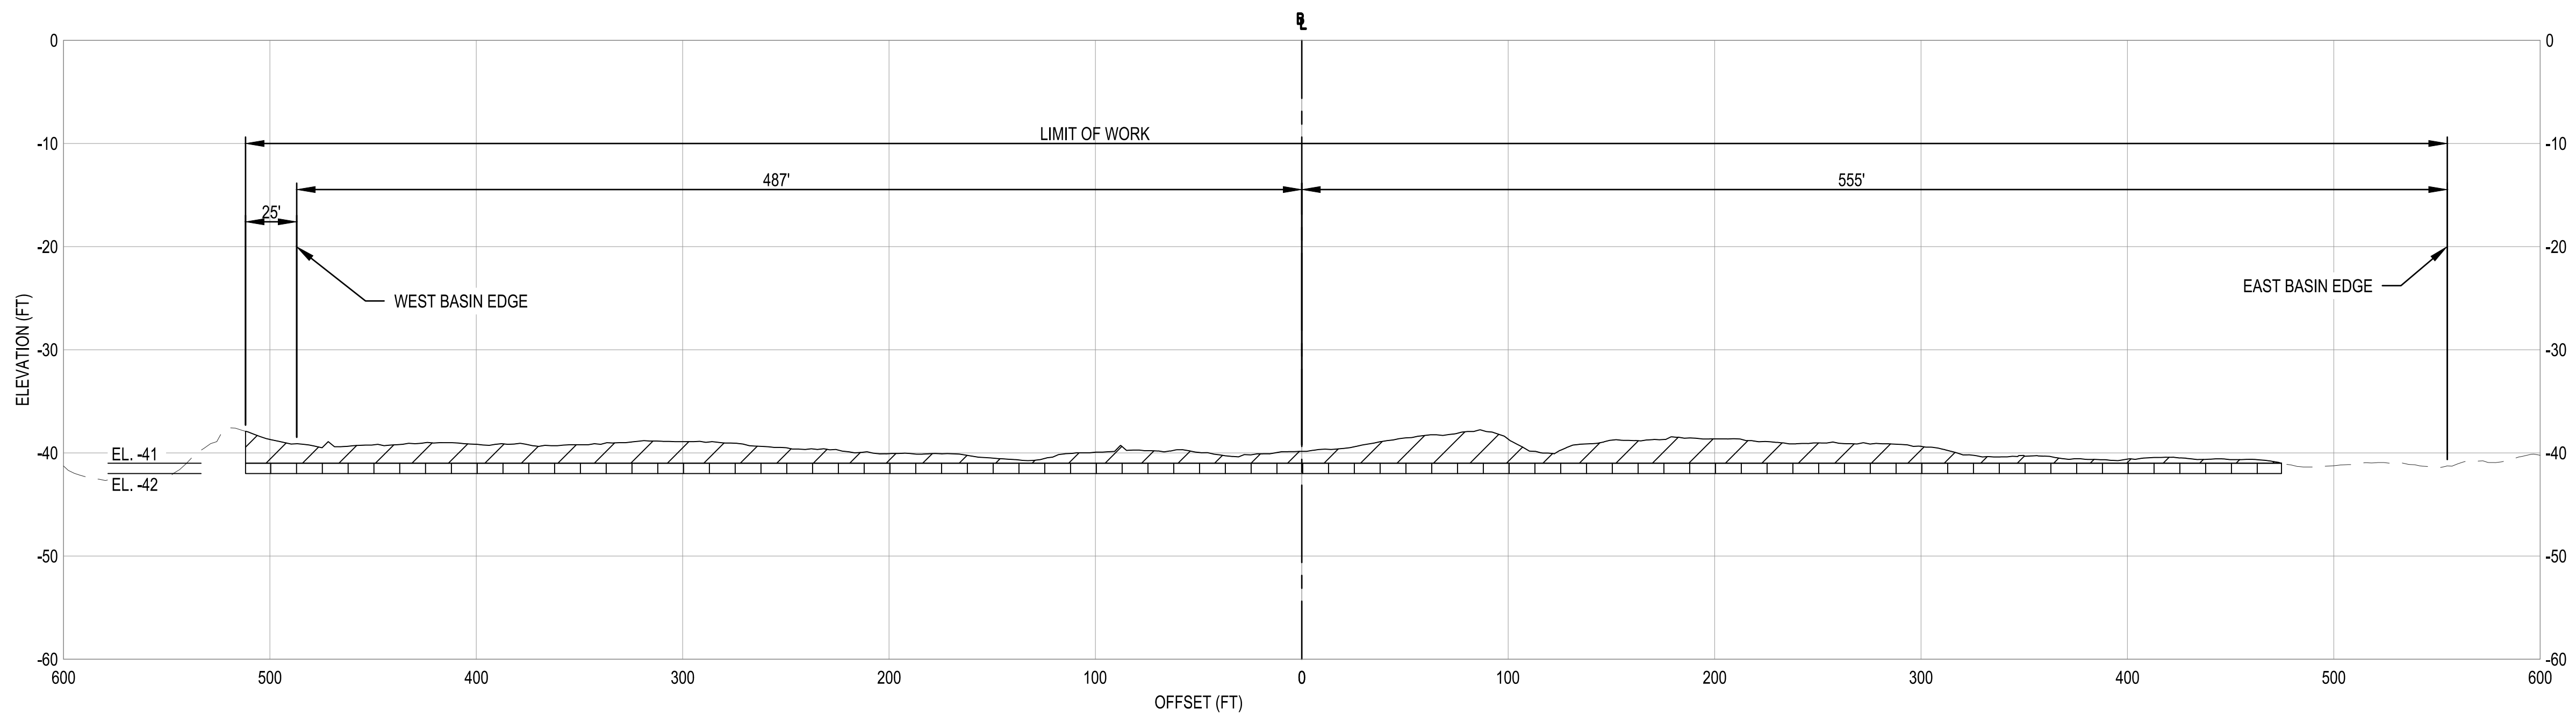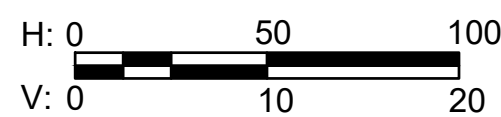


A1 CROSS SECTION - FAIRLESS TURNING BASIN (STA. 0+350)
SCALE IN FEET

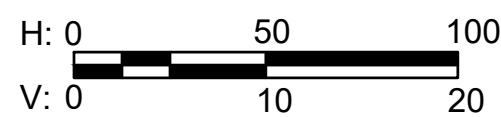[illegible]

U.S. ARMY CORPS OF ENGINEERS PHILADELPHIA DISTRICT	DESIGNED BY:	JUNE 2025	ISSUED/REVISION DATE:
	L.M.WILL	JUNE 2025	
	CHECKED BY:	WJ2BL02800R	CONTRACT NUMBER:
	O.DURR		
	SUBMITTED BY:	PILOT DATE:	
	W.DRUMER	4 June 2025	
	FILE NAME:		
	ANS E 3444		
			C-002 CROSS SECTIONS - FARR TURN BURNING

DELAWARE RIVER
PHILADELPHIA, PENNSYLVANIA TO TRENTON, NEW JERSEY
MAINTENANCE DREDGING
CROSS SECTIONS - FAIRLESS TURNING BASIN

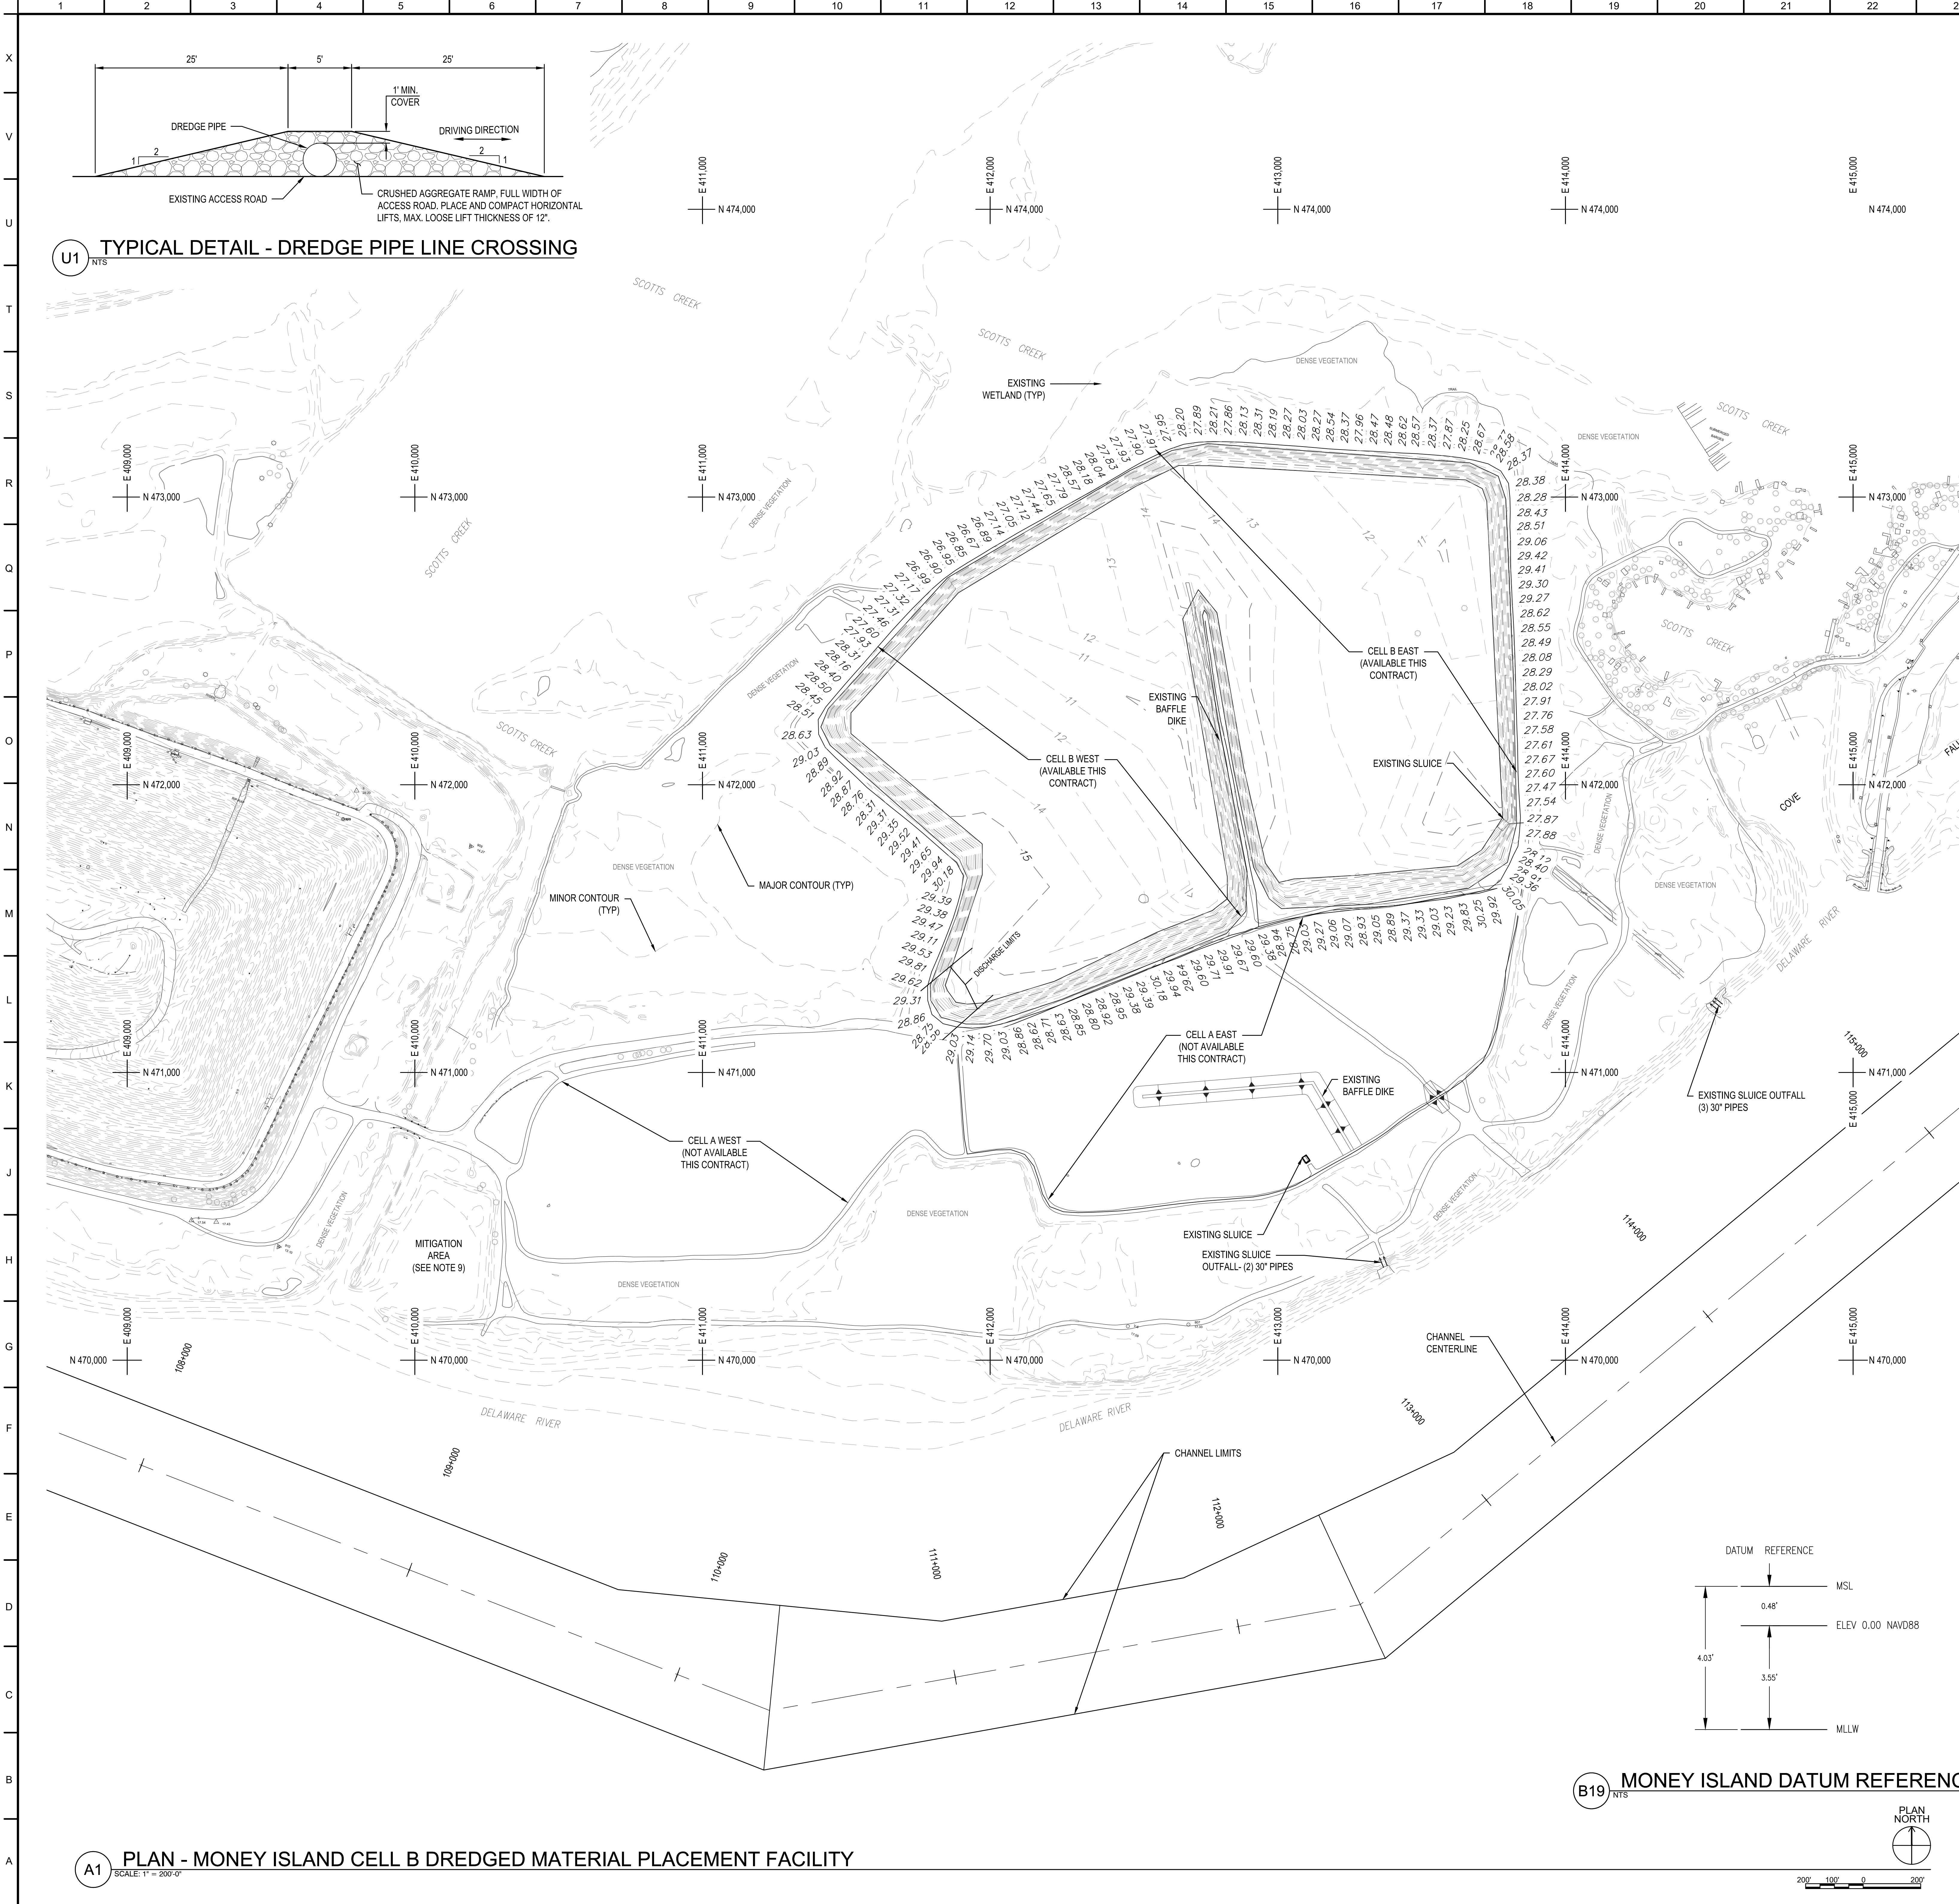

GENERAL NOTES

- VERTICAL DATUM FOR LAND SURVEYS IS BASED ON NATIONAL GEODETIC SURVEY MEAN SEA LEVEL.
- DREDGED MATERIAL HAS BEEN RECENTLY PLACED IN CELL A EAST AND HENCE CONTRACTOR MUST EXERCISE CAUTION USING ONLY LOW GROUND PRESSURE EQUIPMENT WHEN LAYING DISCHARGE LINE TO CELL B EAST.
- WHERE THE DREDGE PIPE LINE CROSSES EXISTING ACCESS ROADS, A RAMP SHALL BE CONSTRUCTED OVER THE PIPE THE FULL WIDTH OF THE ACCESS ROAD, AS SHOWN IN DETAIL U1/C-401.
- THE CONTRACTOR SHALL COORDINATE INGRESS, EGRESS AND ALL CONSTRUCTION ACTIVITIES AT THIS SITE WITH MR. BOB JONES, WASTE MANAGEMENT INC. SITE MANAGER AT MONEY ISLAND, AT (215) 768-4051 PRIOR TO WORK COMMENCEMENT.
- THE CONTRACTOR SHALL NOT ENTER THE MITIGATION AREA.

US Army Corps of Engineers
PHILADELPHIA DISTRICT

KEY PLAN

DESIGNED BY:	DESIGN/INITIAL DATE:	U.S. ARMY CORPS OF ENGINEERS PHILADELPHIA DISTRICT
DRAWN BY:	SOLICITATION NUMBER:	
CHECKED BY:	AWARD NUMBER:	
IN CHARGE BY:	CONTRACT NUMBER:	
DATE:	FILE NAME:	
DATE:	FILE NAME:	

DELaware RIVER
PENNSYLVANIA TO TRENTON, NEW JERSEY
MAINTENANCE DREDGING
PLAN - MONEY ISLAND CELL B DMPF

SHEET ID
C-401