

SYRACUSE VA MEDICAL CENTER

800 IRVING AVENUE
SYRACUSE, NY 13210


PROJECT TITLE:
REPAIR SPS DEFICIENCIES

VA PROJECT NO. 528A7-19-720

INDEX TO DRAWINGS

PAGE	DWG. #	DWG. TITLE
36	MH-101.1	MECHANICAL: NEW GROUND FLOOR HYDRONIC PIPING PLAN - PHASE 4 & 5 ENLARGED PLAN
37	MH-101.2	MECHANICAL: NEW GROUND FLOOR HYDRONIC PIPING PLAN - PHASE 2 ENLARGED PLAN
38	MH-201	MECHANICAL: NEW GROUND FLOOR DUCTWORK PLAN-OVERVIEW PLAN
39	MH-201.1	MECHANICAL: NEW GROUND FLOOR DUCTWORK PLAN - PHASE 4 & 5 ENLARGED PLAN
40	MH-201.2	MECHANICAL: NEW GROUND FLOOR DUCTWORK PLAN - PHASE 2 ENLARGED PLAN
41	MH-301	MECHANICAL: NEW GROUND FLOOR PRESSURE RELATIONSHIP PLAN-OVERVIEW PLAN
42	MH-301.1	MECHANICAL: NEW GROUND FLOOR PRESSURE RELATIONSHIP PLAN - PHASE 4 & 5 ENLARGED PLAN
43	MH-301.2	MECHANICAL: NEW GROUND FLOOR PRESSURE RELATIONSHIP PLAN - PHASE 2 ENLARGED PLAN
44	MH-701	MECHANICAL: DETAILS
45	MH-801	MECHANICAL: SCHEDULES & DETAIL
PLUMBING		
46	PL-001	PLUMBING: SYMBOLS, NOTES & ABBREVIATIONS
47	PL-002	PLUMBING: SITE PLAN
48	PD-100	PLUMBING: DEMOLITION BASEMENT SANITARY & RO WATER PIPING PLAN-OVERVIEW PLAN
49	PD-100.1	PLUMBING: DEMOLITION BASEMENT SANITARY & RO WATER PLAN-PHASE 4 & 5 ENLARGED PLAN
50	PD-100.2	PLUMBING: DEMOLITION BASEMENT SANITARY & RO WATER PLAN-PHASE 2 ENLARGED PLAN
51	PD-101	PLUMBING: DEMOLITION GROUND FLOOR SANITARY PIPING PLAN-OVERVIEW PLAN
52	PD-101.1	PLUMBING: DEMOLITION GROUND FLOOR SANITARY PIPING PLAN-PHASE 4 & 5 ENLARGED PLAN
53	PD-101.2	PLUMBING: DEMOLITION GROUND FLOOR SANITARY PIPING PLAN-PHASE 2 ENLARGED PLAN
54	PD-201	PLUMBING: DEMOLITION GROUND FLOOR DOMESTIC PLAN-OVERVIEW PLAN
55	PD-201.1	PLUMBING: DEMOLITION GROUND FLOOR DOMESTIC PLAN-PHASE 4 & 5 ENLARGED PLAN
56	PD-201.2	PLUMBING: DEMOLITION GROUND FLOOR DOMESTIC PLAN-PHASE 2 ENLARGED PLAN
57	PD-301	PLUMBING: DEMOLITION GROUND FLOOR MED GAS PIPING PLAN-OVERVIEW PLAN
58	PD-301.1	PLUMBING: DEMOLITION GROUND FLOOR MED GAS PIPING PLAN-PHASE 4 & 5 ENLARGED PLAN
59	PD-301.2	PLUMBING: DEMOLITION GROUND FLOOR MED GAS PIPING PLAN-PHASE 2 ENLARGED PLAN
60	PL-100	PLUMBING: NEW BASEMENT SANITARY & RO WATER PLAN-OVERVIEW PLAN
61	PL-100.1	PLUMBING: NEW BASEMENT SANITARY & RO WATER PLAN-PHASE 4 & 5 ENLARGED PLAN
62	PL-100.2	PLUMBING: NEW BASEMENT SANITARY & RO WATER PLAN-PHASE 2 ENLARGED PLAN
63	PL-101	PLUMBING: NEW GROUND FLOOR SANITARY PIPING PLAN-OVERVIEW PLAN
64	PL-101.1	PLUMBING: NEW GROUND FLOOR SANITARY PIPING PLAN-PHASE 4 & 5 ENLARGED PLAN
65	PL-101.2	PLUMBING: NEW GROUND FLOOR SANITARY PIPING PLAN-PHASE 2 ENLARGED PLAN
66	PL-201	PLUMBING: NEW GROUND FLOOR DOMESTIC PLAN-OVERVIEW PLAN
67	PL-201.1	PLUMBING: NEW GROUND FLOOR DOMESTIC PLAN-PHASE 4 & 5 ENLARGED PLAN
68	PL-201.2	PLUMBING: NEW GROUND FLOOR DOMESTIC PLAN-PHASE 2 ENLARGED PLAN
69	PL-301	PLUMBING: NEW GROUND FLOOR MED GAS PIPING PLAN-OVERVIEW PLAN
70	PL-301.1	PLUMBING: NEW GROUND FLOOR MED GAS PIPING PLAN-PHASE 4 & 5 ENLARGED PLAN
71	PL-301.2	PLUMBING: NEW GROUND FLOOR MED GAS PIPING PLAN-PHASE 2 ENLARGED PLAN
72	PL-701	PLUMBING: DETAILS
73	PL-702	PLUMBING: DETAILS
FIRE PROTECTION		
74	FX-001	FIRE PROTECTION: SYMBOLS, NOTES, ABBREVIATIONS & DETAILS
75	FX-002	FIRE PROTECTION: SITE PLAN
76	FXD-101	FIRE PROTECTION: DEMOLITION GROUND FLOOR PLAN-OVERVIEW PLAN
77	FXD-101.1	FIRE PROTECTION: DEMOLITION GROUND FLOOR PLAN-PHASE 4 & 5 ENLARGED PLAN
78	FXD-101.2	FIRE PROTECTION: DEMOLITION GROUND FLOOR PLAN-PHASE 2 ENLARGED PLAN
79	FX-101	FIRE PROTECTION: NEW GROUND FLOOR PLAN-OVERVIEW PLAN
80	FX-101.1	FIRE PROTECTION: NEW GROUND FLOOR PLAN-PHASE 4 & 5 ENLARGED PLAN
81	FX-101.2	FIRE PROTECTION: NEW GROUND FLOOR PLAN-PHASE 2 ENLARGED PLAN
ELECTRICAL		
82	ES-001	ELECTRICAL: SYMBOLS, NOTES & ABBREVIATIONS
83	ES-002	ELECTRICAL: SITE PLAN
84	ED-101	ELECTRICAL: DEMOLITION GROUND FLOOR POWER PLAN-OVERVIEW PLAN
85	ED-101.1	ELECTRICAL: DEMOLITION GROUND FLOOR POWER PLAN-PHASE 4 & 5 ENLARGED PLAN
86	ED-101.2	ELECTRICAL: DEMOLITION GROUND FLOOR POWER PLAN-PHASE 2 ENLARGED PLAN
87	ED-201	ELECTRICAL: DEMOLITION GROUND FLOOR LIGHTING PLAN-OVERVIEW PLAN
88	ED-201.1	ELECTRICAL: DEMOLITION GROUND FLOOR LIGHTING PLAN-PHASE 4 & 5 ENLARGED PLAN
89	ED-201.2	ELECTRICAL: DEMOLITION GROUND FLOOR LIGHTING PLAN-PHASE 2 ENLARGED PLAN
90	ES-101	ELECTRICAL: NEW GROUND FLOOR POWER PLAN-OVERVIEW PLAN
91	ES-101.1	ELECTRICAL: NEW GROUND FLOOR POWER PLAN-PHASE 4 & 5 ENLARGED PLAN
92	ES-101.2	ELECTRICAL: NEW GROUND FLOOR POWER PLAN-PHASE 2 ENLARGED PLAN
93	ES-201	ELECTRICAL: NEW GROUND FLOOR LIGHTING PLAN-OVERVIEW PLAN
94	ES-201.1	ELECTRICAL: NEW GROUND FLOOR LIGHTING PLAN-PHASE 4 & 5 ENLARGED PLAN
95	ES-201.2	ELECTRICAL: NEW GROUND FLOOR LIGHTING PLAN-PHASE 2 ENLARGED PLAN
96	ES-601	ELECTRICAL: ONE-LINE DIAGRAMS
97	ES-701	ELECTRICAL: DETAILS
98	ES-801	ELECTRICAL: SCHEDULES
99	ES-802	ELECTRICAL: SCHEDULES

LOCATION MAP

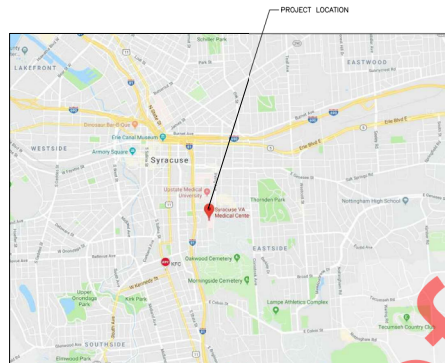

KEY PLAN



INDEX TO DRAWINGS

PAGE	DWG. #	DWG. TITLE
GENERAL		
1	GI-001	TITLE SHEET WITH INDEX TO DRAWINGS
2	GI-002	BASEMENT & GROUND FLOOR CONSTRUCTION ENTRANCE/EXIT
3	GI-003	BASEMENT & GROUND FLOOR FRA PLAN
4	GI-004	GROUND FLOOR PHASING PLAN
5	GI-005	TEMPORARY MOBILES SPS PLAN
6	LS-100	SITE & PARTIAL GROUND FLOOR LIFE SAFETY PLAN
7	LS-101	GROUND FLOOR LIFE SAFETY PLAN & SCHEDULE
ARCHITECTURAL		
8	AS-001	ARCHITECTURAL: SYMBOLS, NOTES & ABBREVIATIONS
9	AS-002	ARCHITECTURAL: SITE PLAN
10	AS-003	ARCHITECTURAL: TEMPORARY STRUCTURE SECTIONS
11	AD-100	ARCHITECTURAL: SMOKING SHELTER DEMOLITION PLAN
12	AD-101	ARCHITECTURAL: DEMOLITION GROUND FLOOR PLAN
13	AD-102	ARCHITECTURAL: DEMOLITION GROUND FLOOR REFLECTIVE CEILING PLAN
14	AS-100	ARCHITECTURAL: PATIO PLAN
15	AS-101	ARCHITECTURAL: NEW GROUND FLOOR PLAN
16	AS-201	ARCHITECTURAL: NEW GROUND FLOOR REFLECTIVE CEILING PLAN
17	AS-301	ARCHITECTURAL: NEW GROUND FLOOR EQUIPMENT PLAN
18	AS-401	ARCHITECTURAL: WALL SECTIONS
19	AS-501	ARCHITECTURAL: ENLARGED FLOOR PLANS & INTERIOR ELEVATIONS
20	AS-502	ARCHITECTURAL: ENLARGED FLOOR PLANS & INTERIOR ELEVATIONS
21	AS-503	ARCHITECTURAL: ENLARGED FLOOR PLANS
22	AS-504	ARCHITECTURAL: INTERIOR ELEVATIONS
23	AS-701	ARCHITECTURAL: DETAILS
24	AS-801	ARCHITECTURAL: SCHEDULES
25	AS-901	ARCHITECTURAL: FLOOR FINISH PLAN
26	AS-902	ARCHITECTURAL: NEW SIGNAGE GROUND FLOOR PLAN
MECHANICAL		
27	MH-001	MECHANICAL: SYMBOLS, NOTES & ABBREVIATIONS
28	MH-002	MECHANICAL: SITE PLAN
29	MD-101	MECHANICAL: DEMOLITION GROUND FLOOR HYDRONIC PIPING PLAN-OVERVIEW PLAN
30	MD-101.1	MECHANICAL: DEMOLITION GROUND FLOOR HYDRONIC PIPING PLAN-PHASE 4 & 5 ENLARGED PLAN
31	MD-101.2	MECHANICAL: DEMOLITION GROUND FLOOR HYDRONIC PIPING PLAN-PHASE 2 ENLARGED PLAN
32	MD-201	MECHANICAL: DEMOLITION GROUND FLOOR DUCTWORK PLAN-OVERVIEW PLAN
33	MD-201.1	MECHANICAL: DEMOLITION GROUND FLOOR DUCTWORK PLAN-PHASE 4 & 5 ENLARGED PLAN
34	MD-201.2	MECHANICAL: DEMOLITION GROUND FLOOR DUCTWORK PLAN-PHASE 2 ENLARGED PLAN
35	MH-101	MECHANICAL: NEW GROUND FLOOR HYDRONIC PIPING PLAN-OVERVIEW PLAN

Revisions:	Date:

CONSULTANT

ENGINEER OF RECORD

FELENERZ
ENGINEERING LLP
FE PROJECT #: 19-263
22 Mulberry St., Suite 2A,
Madison, NY 13840
1-845-343-1481 to 845-343-4999
UNAUTHORIZED ALTERATION OR ADDITION TO A PLAN
BEARING A LICENSED PROFESSIONAL ENGINEER'S SEAL IS
A VIOLATION OF STATE EDUCATION LAW.

STAMP
ERIC D. FELENERZ, P.E.



Office of
Construction and
Facilities
Management

VA U.S. Department of
Veterans Affairs

Drawing Title
TITLE SHEET WITH INDEX TO DRAWINGS

Approved: Project Director



Phase
100% FOR
CONSTRUCTION

Project Title
VA SYRACUSE
REPAIR SPS DEFICIENCIES

Location
VAMC, SYRACUSE, NY
Issue Date
02-21-2025
Checked
EDF
Drawn
SRB

Project Number
528A7-19-720
Building Number
1

Drawing Number
GI-001
PAGE: 1 OF 99

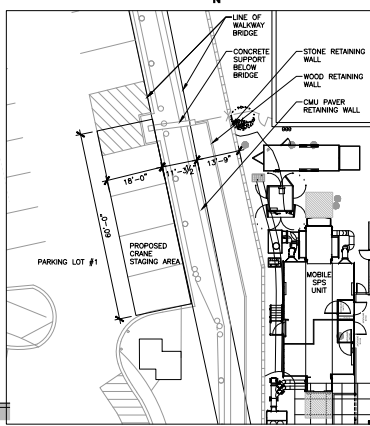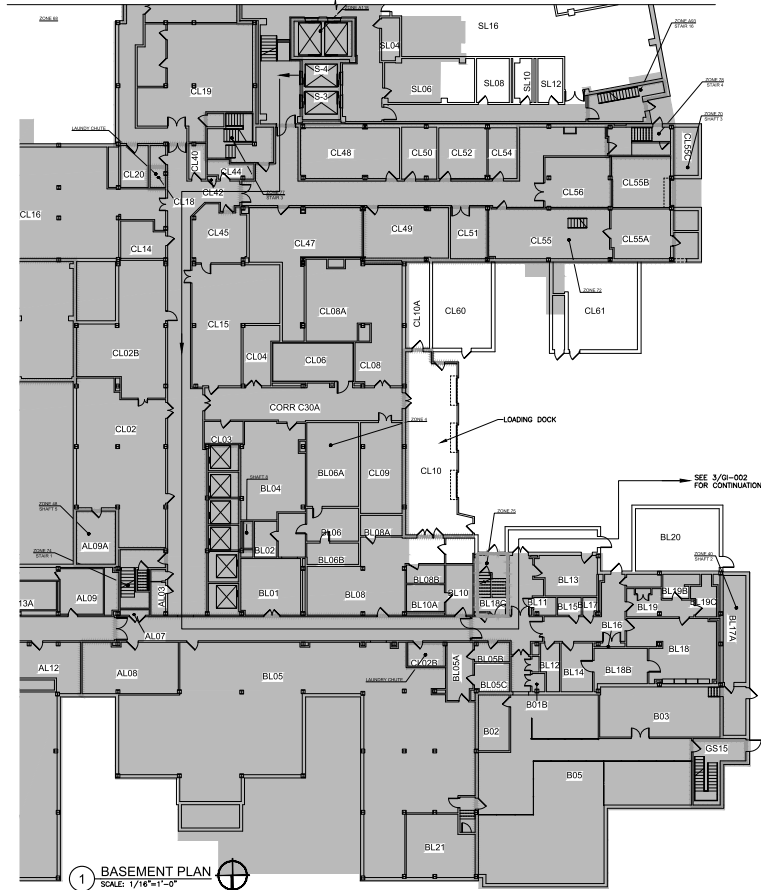

PROJECT NOTES:

1. CONTRACTOR SHALL REMOVE AND STORE ALL VA EQUIPMENT AS SPECIFIED IN THESE DOCUMENTS AND RESTORE IT BACK TO WORKING CONDITION AS SHOWN ON THE DRAWINGS. CONTRACTOR SHALL PROVIDE WELL-CONDITIONED, SAFE STORAGE SPACE FOR THE VA EQUIPMENT THAT IS TO BE RE-INSTALLED. THE STORAGE SHALL NOT BE ON VA PROPERTY AND IT IS THE CONTRACTOR'S RESPONSIBILITY TO MOVE THE VA ITEMS FROM THE VAMC FACILITY TO THE STORAGE SPACE AND BACK TO THE VAMC WHEN RE-INSTALLATION IS REQUIRED. THE CONTRACTOR IS RESPONSIBLE FOR ALL DAMAGE TO VA ITEMS INCURRED DURING REMOVAL, TRANSPORT AND RE-INSTALLATION.
2. ALL MOVEMENT OF EQUIPMENT OR DEBRIS THAT REQUIRES THE USE OF ELEVATORS SHALL BE MOVED DURING OFF HOURS (I.E. MONDAY-FRIDAY 4-8 P.M. OR WEEKENDS), COORDINATE WITH COR.

GENERAL NOTE:

1. THE PLAN ABOVE SHOWS A POSSIBLE LOCATION TO PLACE A CONTRACTOR'S DUMPER. THE AVAILABILITY OF THE SPACE DURING THE TIME OF CONSTRUCTION MUST BE COORDINATED WITH THE PROJECT'S COR IN ORDER TO HAVE THAT DUMPER SPOT ASSIGNED TO THEM. DUMPER SHALL OCCUPY ONE (1) SPACE ONLY IN PARKING LOT #1 & LOT #2. DUMPER IN PARKING LOT #1 SHALL REMAIN FOR A PERIOD OF ONE (1) MONTH ONLY.
2. PROPOSED STAGING AREA FOR ANY CRANE AND LIFTING EQUIPMENT. THE AVAILABILITY OF THE SPACE DURING THE TIME OF CONSTRUCTION MUST BE COORDINATED WITH THE PROJECT'S COR. CONTRACTOR SHALL PROVIDE ALL SECURITY AND PERSONNEL REQUIRED TO PERFORM LIFT SAFELY.
3. PROPOSED LIMITED TIME (2 DAYS MAX.) STAGING AREA FOR SPS UNIT PRIOR TO LIFT. COORDINATE WITH THE PROJECT'S COR.
4. ALL CRANE ACTIVITY SHALL TAKE PLACE ON SATURDAY OR SUNDAY.
5. CONTRACTOR SHALL OBTAIN ALL REQUIRED PERMITS, IF NEEDED, FROM CITY OF SYRACUSE.
6. STREET SIGN TO BE TEMPORARILY REMOVED FOR CRANE ENTRY AND EXIT FOR PROPOSED ROUTE SHOWN. RE-INSTALL AFTER CRANE EXITS SITE.
7. PROVIDE BLOCKING AT ALL CRANE CURB CROSSING AREAS.

3 SITE PLAN
 SCALE: 1/64"=1'-0"

4 ENLARGED SITE PLAN
 SCALE: 1/16"=1'-0"

Revisions:	Date:

CONSULTANT

ENGINEER OF RECORD

FELENERZ
 ENGINEERING LLP
 FE PROJECT #: 19-205
 22 Hubbard St., Suite 2A,
 Madison, NY 13060
 1-800-343-1481 or 605-343-4986
 www.felengr.com
 181 Church St., Suite 100,
 Philadelphia, NY 13020
 1-800-654-8754 or 605-320-8755
 UNAUTHORIZED ALTERATION OR ADDITION TO A PLAN
 BEARING A LICENSED PROFESSIONAL ENGINEER'S SEAL
 IS A VIOLATION OF STATE EDUCATION LAW.

STAMP
 ERIC D. FELENERZ, P.E.



**Office of
 Construction
 and Facilities
 Management**



Drawing Title
 BASEMENT & GROUND FLOOR
 CONSTRUCTION ENTRANCE / EXIT

Approved: Project Director


Phase
 100% FOR
 CONSTRUCTION

Project Title
 VA SYRACUSE
 REPAIR SPS DEFICIENCIES


Location
 VAMC, SYRACUSE, NY
 Issue Date
 02-21-2025
 Checked
 EDF
 Drawn
 SRB

Project Number
 528A7-19-720
 Building Number
 1

Drawing Number
 GI-002
 PAGE: 2 OF 99

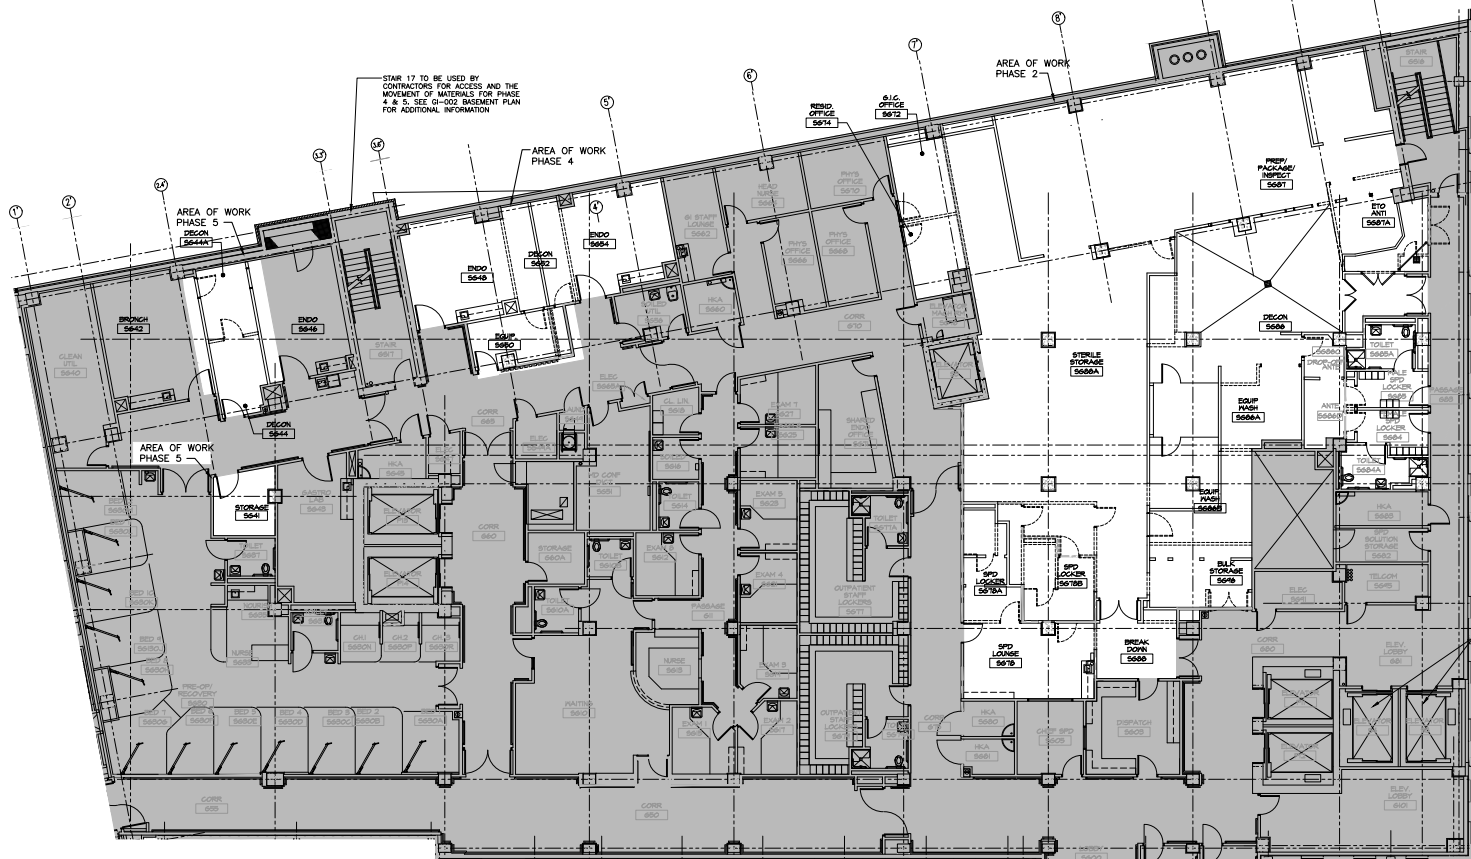

1 GROUND FLOOR PHASING PLAN
SCALE: 1/8"=1'-0"

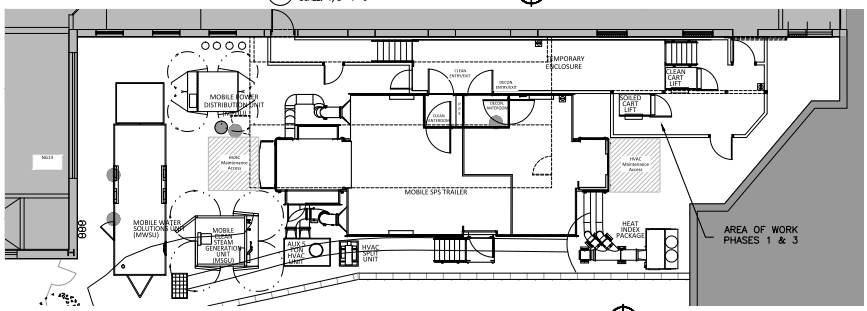

2 TEMPORARY MOBILE SPS SITE PHASING PLAN
SCALE: 1/8"=1'-0"

- PHASING PLAN:**
- PHASE 1 - TEMPORARY SPS OUTDOOR UNITS**
- 1A. DEMOLISH THE EXISTING SMOKING SHELTER AND PREPARE THE SITE FOR THE SPS OUTDOOR UNITS. ROUTE ALL UTILITIES THROUGH THE BUILDING TO OUTSIDE FOR CONNECTION INTO THE SPS UNITS BEFORE DELIVERY. CONSTRUCT THE OUTDOOR TEMPORARY ENCLOSURE.
 - 1B. DELIVERY AND SET-UP OF SPS UNITS OUTSIDE WITH CONNECTIONS TO UTILITIES.
 - ESTIMATED TIME DURATION 1A: 8 WEEKS
 - ESTIMATED TIME DURATION 1B: 2 WEEKS
- PHASE 2:**
- SHEAT DOWN AREAS SHOWN TO BE WORKED ON CONCURRENTLY ONCE THE TEMPORARY MOBILE SPS UNIT IS COMPLETELY OPERATIONAL. THIS PHASE CONSISTS OF ALL EQUIPMENT REMOVAL, DEMOLITION, NEW CONSTRUCTION AND EQUIPMENT RELOCATION WORK AS SHOWN ON THE DRAWINGS. THE NEW ROOMS WILL BE CREATED INSIDE OF EXISTING ROOM SPACE. PHASE 2 WORK SHALL NOT START UNTIL PHASES 1A AND 1B ARE COMPLETED.
 - ESTIMATED TIME DURATION: 24 WEEKS
- PHASE 3 - TEMPORARY SPS OUTDOOR UNITS**
- DECOMMISSIONING AND REMOVAL OF SPS UNITS OUTSIDE ONCE PHASE 2 IS COMPLETED. RESTORE THE SITE TO ORIGINAL (SLAB WITH NO SMOKING SHELTER) CONDITION. THIS INCLUDES DEMOLISHING THE ENCLOSED OUTDOOR TEMPORARY ENCLOSURE, UTILITIES AND ALL APPURTENANCES.
 - ESTIMATED TIME DURATION: 4 WEEKS
- PHASE 4:**
- SHEAT DOWN AREAS SHOWN FOR PHASE 4 WORK ONLY AFTER PHASE 3 IS COMPLETED. THIS PHASE CONSISTS OF ALL EQUIPMENT REMOVAL, DEMOLITION, NEW CONSTRUCTION AND EQUIPMENT RELOCATION WORK AS SHOWN ON THE DRAWINGS.
 - ESTIMATED TIME DURATION: 3 WEEKS
- PHASE 5:**
- SHEAT DOWN AREAS SHOWN FOR PHASE 5 WORK ONLY AFTER PHASE 4 IS COMPLETED. EQUIPMENT REMOVAL, DEMOLITION AND NEW CONSTRUCTION SHALL BE COMPLETED IN SGH, SGH-A, SGH-B AND SGH-C FIRST. EQUIPMENT RELOCATION FROM SGH TO SGH SHALL THEN BE COMPLETED, FOLLOWED BY THE DEMOLITION, NEW CONSTRUCTION AND EQUIPMENT RELOCATION FOR SGH.
 - ESTIMATED TIME DURATION: 3 WEEKS


- GENERAL PHASING NOTES:**
- PHASES 1 & 3 WILL REQUIRE THE USE OF A CRANE OR A LIFT TO INSTALL AND REMOVE EQUIPMENT. THE CONTRACTOR SHALL BE RESPONSIBLE FOR REVIEWING THE SET AND PROVIDING A LIFTING PLAN TO THE COR FOR REVIEW AND APPROVAL.
 - ALL MOVEMENT OF EQUIPMENT OR DEBRIS THAT REQUIRES THE USE OF ELEVATORS SHALL BE MOVED DURING OFF HOURS (I.E. MONDAY-FRIDAY 4 PM OR WEEKENDS), COORDINATE WITH COR.

SERVICE ELEVATORS TO BE USED BY CONTRACTORS FOR ACCESS AND THE MOVEMENT OF MATERIALS FOR PHASE 2. SEE GENERAL PHASING NOTE 2 FOR ADDITIONAL INFORMATION

File Name: F:\2018\10\20\SPS DEFICIENCY REPAIR_VA SYRACUSE\GSDM.dwg (Layout: 01.dwg)
Date: Thu, 10/20/2023 1:14 PM (User: JG)

Revisions:	Date:

CONSULTANT 2214 Berry St., Suite 2A, Washington, MO 63090 1-800-343-1481 N. 840-343-4996	ENGINEER OF RECORD FELTZNER ENGINEERING LLP FE PROJECT #: 19-263 181 Church St., Suite 100, Pittsburgh, PA 15203 1-800-654-0754 N. 855-200-8775 UNAUTHORIZED ALTERATION OR ADDITION TO A PLAN BEARING A LICENSED PROFESSIONAL ENGINEER'S SEAL IS A VIOLATION OF STATE EDUCATION LAW.	STAMP ERIC D. FELLNER, P.E. Office of Construction and Facilities Management VA U.S. Department of Veterans Affairs	Drawing Title GROUND FLOOR PHASING PLAN Approved: Project Director	Phase 100% FOR CONSTRUCTION	Project Title VA SYRACUSE REPAIR SPS DEFICIENCIES Location VAMC, SYRACUSE, NY Issue Date 02-21-2025	Project Number 528A7-19-720 Building Number 1 Drawing Number GI-004 PAGE: 4 OF 99
			Checked EDF	Drawn SRB	Checked EDF	Drawn SRB

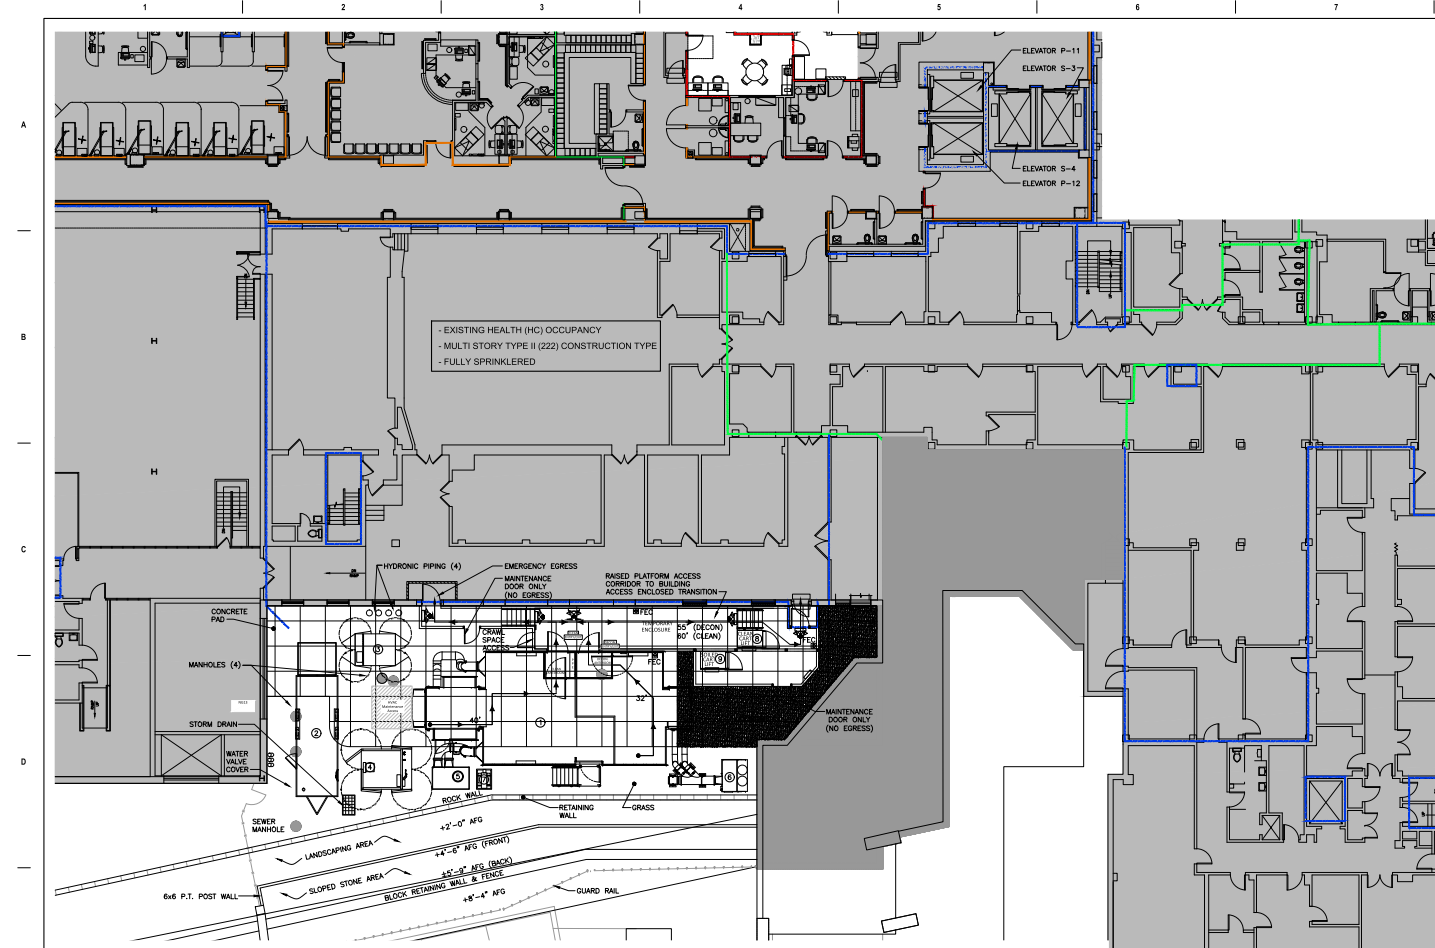

APPLICABLE CODE SECTIONS PER VA FIRE PROTECTION DESIGN MANUAL - JUNE 1, 2021 (VA FPM) AREAS MUST BE SPRINKLERED.

2.2 BUILDING SEPARATION DISTANCE:

A. THE REQUIREMENT FOR FIRE RESISTANCE RATINGS OF EXTERIOR WALLS, MASONRY AREA FOR EXTERIOR WALL OPENINGS, AND OPENING PROTECTION MUST COMPLY WITH IBC (SEE NOTE 1) EXCEPT AS FOLLOWS:

1. THERE ARE NO REQUIREMENTS FOR SEPARATION OR OPENINGS BETWEEN VA BUILDINGS WHEN BOTH (ALL) BUILDINGS ARE FULLY SPRINKLERED (SEE NOTE 3). THIS EXCEPTION DOES NOT APPLY TO VA BUILDINGS THAT ARE ADJACENT TO NON-VA PROPERTY LINES.

2.2.A.2 NOTE 3. IF BUILDINGS TOUCH EACH OTHER, ADDITIONAL REQUIREMENTS MIGHT APPLY. FOR BUILDINGS OF DIFFERENT CONSTRUCTION TYPES THAT ARE CONNECTED, CLASSIFICATION OF THE STRUCTURE TO BE THE LEAST FIRE-RESISTIVE CONSTRUCTION TYPE OF THE CONNECTED PORTIONS UNLESS THERE IS A 2-HOUR OR GREATER VERTICALLY-ALIGNED FIRE BARRIER WALL BETWEEN THE PORTIONS OF THE BUILDING IN ACCORDANCE WITH NFPA 221. IN ADDITION, NFPA 221, 7.3.1 DOES NOT PERMIT WINDOWS IN THE TWO HOUR OR GREATER RATED FIRE BARRIER WALL.

LIFE SAFETY LEGEND:

- SMOKE BARRIER - 1 HR FIRE RATED
- CORRIDOR WALL - SMOKE PARTITION - 0 HR FIRE RATED (LIMIT TRANSFER OF SMOKE)
- 1 HR FIRE RATED BARRIER (45 MINUTE DOORS)
- 2 HR FIRE RATED BARRIER (1-1/2 HR DOOR AND FIRE DAMPERS)
- DISTANCE TO EXIT
- LOCATION OF NEW TEMPORARY FIRE EXTINGUISHER CABINET WITH 10LB EXTINGUISHER (26 GALLON PER MINUTE SURFACE MOUNTED (L.A.C.) MINIMUM INTERIOR DIMENSIONS: 9'x4'x27". FIRE EXTINGUISHER TO BE PROVIDED BY VA. MOUNT BOTTOM OF CABINET 36" AFF.
- NEW TEMPORARY EXIT SIGN
- LOCATION WITH EMERGENCY BATTERY BACK-UP LIGHTS
- DENOTES DIRECTION

LIFE SAFETY INFORMATION AS PER NFPA 101-2021:
 EXISTING BUILDING CONSISTS OF HEALTH CARE (HC) OCCUPANCY.
 EXISTING BUILDING IS MULTI STORY CONSTRUCTION TYPE II (222)

NEW SQUARE FOOTAGE IS: 1,514 SF
 TOTAL SQUARE FOOTAGE IS: 1,514 SF

CONSTRUCTION TYPE LIMITATIONS (NFPA 101 TABLE 19.1.6.1)

CONSTRUCTION TYPE	SPRINKLERED	TOTAL NUMBER OF STORES OF BUILDING
		1 2 3 4
I (442)	YES	X X X X
	NO	X X X X
I (232)	YES	X X X X
	NO	X X X X
II (222)	YES	X X X X
	NO	X X X X
II (111)	YES	X X X X
	NO	X X X X
II (000)	YES	X X X X
	NO	X X X X
II (211)	YES	X X X X
	NO	X X X X
II (200)	YES	X X X X
	NO	X X X X
IV (240)	YES	X X X X
	NO	X X X X
V (111)	YES	X X X X
	NO	X X X X
V (000)	YES	X X X X
	NO	X X X X

NOTES:

- X=PERMITTED, NP=NOT PERMITTED
- THE TOTAL NUMBER OF STORES OF THE BUILDING IS TO BE DETERMINED AS FOLLOWS:
 A. THE TOTAL NUMBER OF STORES IS TO BE COUNTED STARTING WITH THE LEVEL OF EXIT DISCHARGE AND ENDING WITH THE HIGHEST OCCUPABLE STORY OF THE BUILDING.
 B. STORES BELOW THE LEVEL OF EXIT DISCHARGE ARE NOT COUNTED AS STORES.
 C. INTERSTITIAL SPACES USED SOLELY FOR BUILDING OR PROCESS SYSTEM DIRECTION RELATED TO THE LEVEL ABOVE OR BELOW ARE NOT COUNTED AS A SEPARATE STORY.
 D. A MEZZANINE IN ACCORDANCE WITH 8.6.9 IS NOT COUNTED AS A STORY.
- SPRINKLERED THROUGHOUT BY AN APPROVED, SUPPLEMENTED AUTOMATIC SPRINKLER SYSTEM IN ACCORDANCE WITH SECTION 9.7 (SEE 19.3.5)
- BASEMENTS ARE NOT COUNTED AS STORES.

OCCUPANT LOAD

TOTAL OCCUPANT LOAD: 12 OCCUPANTS

CODE REQUIREMENTS FOR HEALTH CARE OCCUPANCY

COMMON PATH OF EGRESS (WITH SPRINKLERS)	100 FT MAX	(N/A)
MAXIMUM DEAD END (WITH SPRINKLERS)	30 FT MAX	(N/A)
TRAVEL DISTANCE (WITH SPRINKLERS)	200 FT MAX	(DESIGN COMPLIES)

FIRE PROTECTION OF BUILDING ELEMENTS FOR TYPE II (222) BUILDING

EXTERIOR BEARING WALLS	1HR RECD
COLUMNS	1HR RECD
BEAMS, TRUSSES AND GIRDERS	1HR RECD
FLOOR-CEILING ASSEMBLIES	2HR RECD
ROOF-CEILING ASSEMBLIES	1HR RECD
INTERIOR NON-BEARING WALLS	0HR RECD

FIRE PROTECTION OF BUILDING ELEMENTS FOR TYPE V (000) BUILDING

EXTERIOR BEARING WALLS	0HR RECD
COLUMNS	0HR RECD
BEAMS, TRUSSES AND GIRDERS	0HR RECD
FLOOR-CEILING ASSEMBLIES	0HR RECD
ROOF-CEILING ASSEMBLIES	0HR RECD
INTERIOR NON-BEARING WALLS	0HR RECD

NOTE:

TYPE V CHART IS APPLICABLE IF 2HR FIRE RATED BARRIER IS SEPARATING EXTERIOR ENCLOSURE AND EXISTING HOSPITAL EXTERIOR WALL.

ACCESSIBLE ROUTE WIDTH

SUB DIVISION OF BUILDING SPACES NO SPECIAL REQUIREMENTS

FIRE PROTECTION SYSTEM:

STRUCTURE SHALL BE FULLY SPRINKLERED.

FIRE EXTINGUISHERS: 2022 NFPA 10

TOTAL NEW FLOOR AREA: 1,514 SF - LIGHT HAZARD OCCUPANCY - HEALTH CARE

MAXIMUM OF 3,000 SF PER UNIT OF 'A', '1' UNIT OF 'A' REQUIRED

MAXIMUM TRAVEL DISTANCE TO EXTINGUISHER 75'

(2 NEW FCC SHOWING)

TAG	DESCRIPTION	FURNISHED AND INSTALLED BY	CONNECTION BETWEEN VA FACILITY & EQUIPMENT BY	CONNECTION BETWEEN EQUIPMENT & MOBILE SPS TRAILER BY	POWER SUPPLY
1	MOBILE SPS TRAILER	MOBILE SPS MANUFACTURER	CONTRACTOR	MOBILE SPS MANUFACTURER	FROM MOBILE POWER DISTRIBUTION UNIT
2	MOBILE WATER SOLUTIONS UNIT (MWSU)	MOBILE SPS MANUFACTURER	CONTRACTOR	MOBILE SPS MANUFACTURER	FROM MOBILE POWER DISTRIBUTION UNIT
3	MOBILE POWER DISTRIBUTION UNIT (MPDU)	MOBILE SPS MANUFACTURER	CONTRACTOR	MOBILE SPS MANUFACTURER	FROM VA HOSPITAL, SEE ES-002
4	MOBILE CLEAN STEAM GENERATION UNIT (MSGU)	MOBILE SPS MANUFACTURER	---	CONTRACTOR	FROM MOBILE POWER DISTRIBUTION UNIT
5	AUX 5 TON HVAC UNIT	MOBILE SPS MANUFACTURER	---	MOBILE SPS MANUFACTURER	FROM MOBILE POWER DISTRIBUTION UNIT
6	HEAT INDEX PACKAGE	MOBILE SPS MANUFACTURER	---	MOBILE SPS MANUFACTURER	FROM MOBILE POWER DISTRIBUTION UNIT
7	HVAC SPLIT UNIT	MOBILE SPS MANUFACTURER	---	MOBILE SPS MANUFACTURER	FROM MOBILE POWER DISTRIBUTION UNIT
8	CLEAN CART LIFT	MOBILE SPS MANUFACTURER	CONTRACTOR	MOBILE SPS MANUFACTURER	FROM MOBILE POWER DISTRIBUTION UNIT
9	SOILED CART LIFT	MOBILE SPS MANUFACTURER	CONTRACTOR	MOBILE SPS MANUFACTURER	FROM MOBILE POWER DISTRIBUTION UNIT

NOTE:

1. THE ABOVE LEGEND AND SCHEDULE IS TYPICAL FOR AN INSTALLATION OF THIS TYPE. THE CONTRACTOR SHALL BE RESPONSIBLE FOR COORDINATING ALL CONTRACT REQUIREMENTS WITH THE TEMPORARY MOBILE SPS MANUFACTURER. SHOULD THE TEMPORARY MOBILE SPS MANUFACTURER NOT PROVIDE ONE OF THE FOLLOWING IN THE LEGEND AND SCHEDULE ABOVE, IT SHALL BECOME THE RESPONSIBILITY OF THE CONTRACTOR TO PROVIDE THE MISSING MATERIAL AND LABOR. THE VA IS NOT RESPONSIBLE FOR ANY PURCHASING OF EQUIPMENT AND HOOKUPS TO THE TEMPORARY EQUIPMENT. ALL CONNECTIONS TO EXISTING FACILITY UTILITIES SHALL BE COORDINATED WITH THE COR.


Revisions:	Date:

CONSULTANT

ENGINEER OF RECORD

FELENER ENGINEERING LLP
 FE PROJECT #: 19-263
 22 Hubbard St., Suite 2A, Pittsburgh, PA 15201
 1-800-343-1481 / 412-343-4886 / 412-343-4887

STAMP

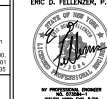

Office of Construction and Facilities Management
 VA U.S. Department of Veterans Affairs

Drawing Title

SITE & PARTIAL GROUND FLOOR LIFE SAFETY PLAN

Approved: Project Director

Phase

100% FOR CONSTRUCTION

Project Title

VA SYRACUSE REPAIR SPS DEFICIENCIES

Location: VAMC, SYRACUSE, NY

Issue Date: 02-21-2025

Checked: EDF

Drawn: SRB

Project Number

528A7-19-720


Building Number: 1

Drawing Number: LS-100


PAGE: 6 OF 99

2 MOUNTING HEIGHTS OF FIRE EXTINGUISHERS

N.F.S.

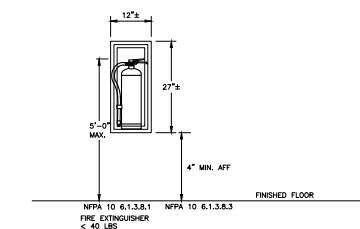

File Name: F:\2019\13-2019 SPS DEFICIENCY REPAIR, VA SYRACUSE\LS-101.dwg (Layout: LS-101)
Date: Thu, 02/21/2025, 11:47 AM (User: JAG)

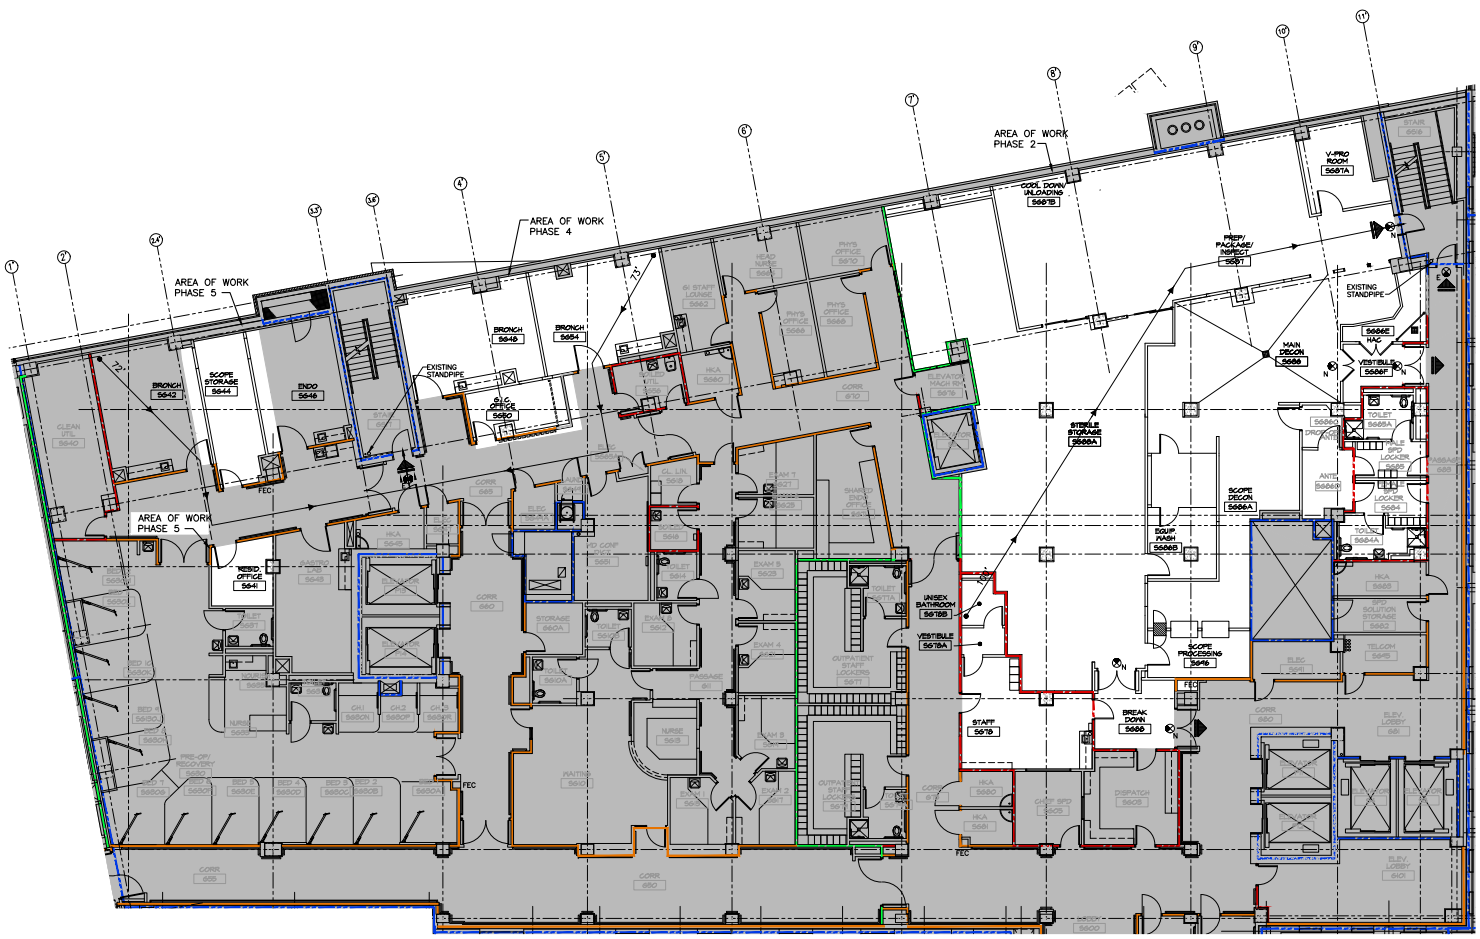

- LIFE SAFETY LEGEND:**
- SMOKE BARRIER - 1 HR FIRE RATED
 - CORRIDOR WALL - SMOKE PARTITION - 0 HR FIRE RATED (LIMIT TRANSFER OF SMOKE)
 - 1 HR FIRE RATED BARRIER (OS MINUTE DOOR)
 - 2 HR FIRE RATED BARRIER (1-1/2 HR DOOR AND FIRE DAMPERS)
 - DISTANCE TO EXIT
 - EXIT
 - FIRE EXTINGUISHER CABINET
 - EXIT SIGN
 - 7" DENOTES EXISTING TO REMAIN
 - Y DENOTES NEW
 - 1 DENOTES DIRECTION

NOTE:
1. REFER TO DRAWING LS-100 FOR SUMMARY OF APPLICABLE CODES.

1 ARCHITECTURAL: GROUND FLOOR LIFE SAFETY PLAN
SCALE: 1/8"=1'-0"

Revisions:	Date:

CONSULTANT

ENGINEER OF RECORD
FELLENER
ENGINEERING LLP
FE PROJECT #: 19-263
22 Oakberry St., Suite 2A,
Madisonville, MO 64650
1-866-343-1481 or 866-343-4866
UNAUTHORIZED ALTERATION OR ADDITION TO A PLAN
BEARING A LICENSED PROFESSIONAL ENGINEER'S SEAL
IS A VIOLATION OF STATE EDUCATION LAW.

STAMP
ERIC D. FELLENER, P.E.
Professional Engineer
State of Missouri
No. 0000000000
Exp. 12/31/2025


Office of
Construction
and Facilities
Management
VA U.S. Department
of Veterans Affairs

Drawing Title
GROUND FLOOR LIFE SAFETY PLAN
& SCHEDULE
Approved: Project Director

Phase
100% FOR
CONSTRUCTION

Project Title
VA SYRACUSE
REPAIR SPS DEFICIENCIES
Location
VAMC, SYRACUSE, NY
Issue Date
02-21-2025
Checked
EDF
Drawn
SRB

Project Number
528A7-19-720
Building Number
1
Drawing Number
LS-101
PAGE: 7 OF 99

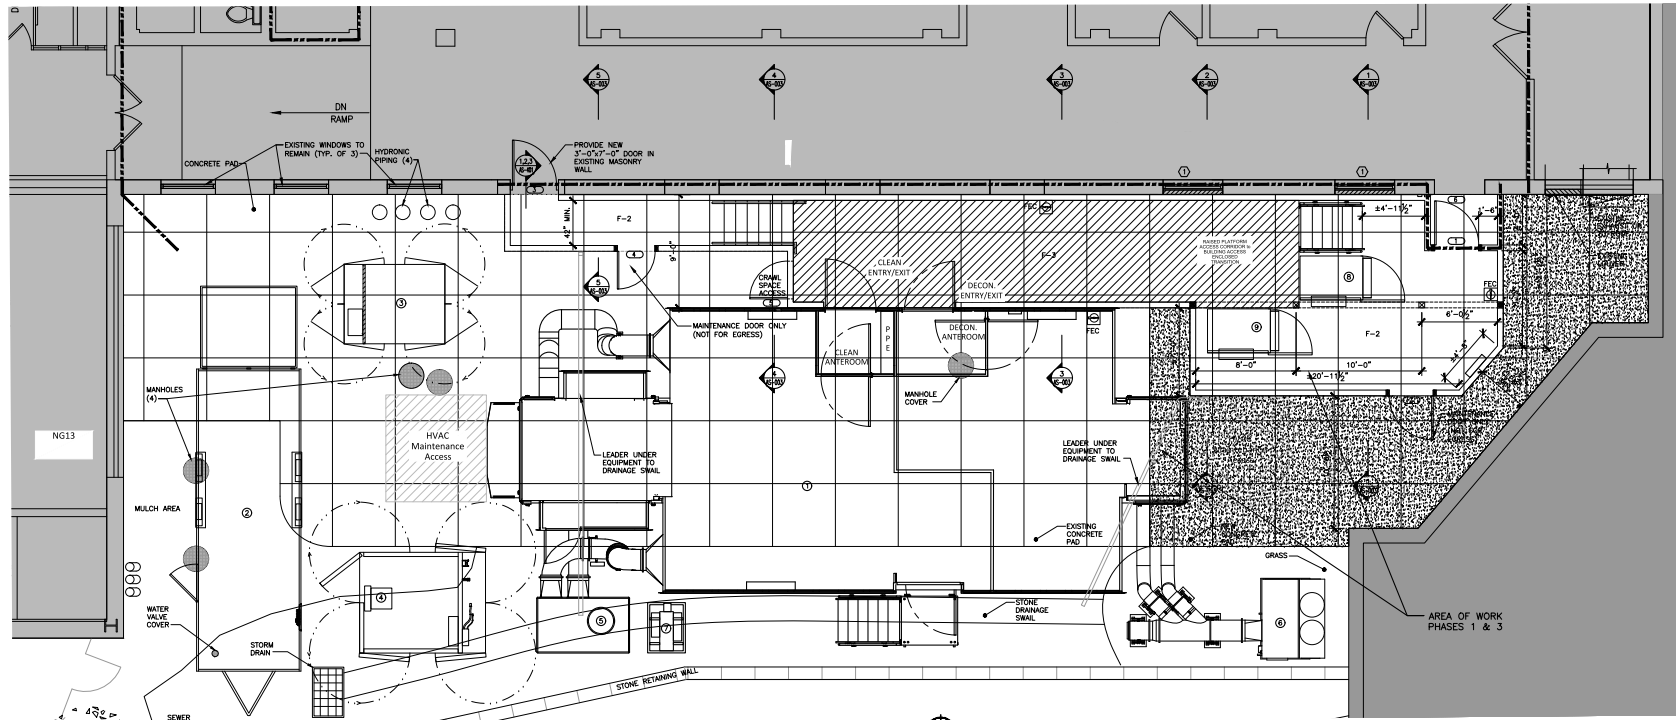

1 SITE PLAN
SCALE: 1/4"=1'-0"

FLOOR PLAN LEGEND	
	EXISTING AREA TO REMAIN (NOT IN SCOPE)
	AREA IN SCOPE
	EXISTING WALL TO REMAIN
	EXISTING DOOR TO REMAIN
	EXISTING CASEWORK TO REMAIN
	EXISTING WALL TO BE REMOVED
	EXISTING DOOR TO BE REMOVED
	EXISTING CASEWORK/CONCRETE TO BE REMOVED
	NEW WALL
	NEW DOOR
	NEW CASEWORK/CONCRETE
	PLUMBING FIXTURES TO REMAIN
	PLUMBING FIXTURES TO BE REMOVED
	NEW PLUMBING FIXTURES
RCP LEGEND	
	EXISTING GRID/CEILING TILE TO REMAIN
	EXISTING GYPSUM CEILING TO REMAIN
	EXISTING GRID/CEILING TILE TO BE REMOVED
	EXISTING GYPSUM CEILING TO BE REMOVED
	NEW GRID/2'x4' CEILING TILE
	NEW GYPSUM CEILING
	EXISTING SUPPLY TO REMAIN
	EXISTING RETURN TO REMAIN
	EXISTING EXHAUST TO REMAIN
	FIRE SPRINKLER HEAD TO REMAIN
	EXISTING 2'x2' LIGHT TO REMAIN
	EXISTING 2'x4' LIGHT TO REMAIN
	2'x2 ACCESS PANEL
	2'x4 ACCESS PANEL
	CEILING MOUNTED SPEAKER
	CEILING MOUNTED EXIT SIGN

KEYED NOTES:

1. PROVIDE 2HR RATED WINDOW IN FILL W/ METAL STUDS AND TWO (2) LAYERS TYPE "X" MOISTURE RESISTANT GYPSUM BOARD W/ EXTERIOR LATEX PAINT. PROVIDE SEALANT AND FIRESTOP AT ALL JOINTS. RESTORE TO ORIGINAL CONDITION UPON REMOVAL OF OUTDOOR TEMPORARY ENCLOSURE.

GENERAL NOTE:

1. THE CONTRACTOR IS RESPONSIBLE FOR ALL SITE VERIFICATIONS AND MEASUREMENTS.

2. CONTRACTOR SHALL PROVIDE GROUT, BACKER ROD, SEALANT AND ALL NECESSARY MATERIALS TO SEAL TEMPORARY WOOD SOLE PLATE OF TEMPORARY ENCLOSURE TO EXISTING AND NEW CONCRETE SURFACES, INCLUDING AT ALL JOINTS.

3. TEMPORARY ENCLOSURE SHALL BE WEATHER TIGHT.

LEGEND & SCHEDULE OF EXTERIOR MOBILE TEMPORARY SPS EQUIPMENT					
TAG	DESCRIPTION	FURNISHED AND INSTALLED BY	CONNECTION BETWEEN VA FACILITY & EQUIPMENT BY	CONNECTION BETWEEN EQUIPMENT & MOBILE SPS TRAILER BY	POWER SUPPLY
1	MOBILE SPS TRAILER	MOBILE SPS MANUFACTURER	CONTRACTOR	MOBILE SPS MANUFACTURER	FROM MOBILE POWER DISTRIBUTION UNIT
2	MOBILE WATER SOLUTIONS UNIT (MWSU)	MOBILE SPS MANUFACTURER	CONTRACTOR	MOBILE SPS MANUFACTURER	FROM MOBILE POWER DISTRIBUTION UNIT
3	MOBILE POWER DISTRIBUTION UNIT (MPDU)	MOBILE SPS MANUFACTURER	CONTRACTOR	MOBILE SPS MANUFACTURER	FROM VA HOSPITAL-SEE ES-002
4	MOBILE CLEAN STEAM GENERATION UNIT (MSGU)	MOBILE SPS MANUFACTURER	---	CONTRACTOR	FROM MOBILE POWER DISTRIBUTION UNIT
5	AUX 5 TON HVAC UNIT	MOBILE SPS MANUFACTURER	---	MOBILE SPS MANUFACTURER	FROM MOBILE POWER DISTRIBUTION UNIT
6	HEAT INDEX PACKAGE	MOBILE SPS MANUFACTURER	---	MOBILE SPS MANUFACTURER	FROM MOBILE POWER DISTRIBUTION UNIT
7	HVAC SPLIT UNIT	MOBILE SPS MANUFACTURER	---	MOBILE SPS MANUFACTURER	FROM MOBILE POWER DISTRIBUTION UNIT
8	CLEAN CART LIFT	MOBILE SPS MANUFACTURER	CONTRACTOR	MOBILE SPS MANUFACTURER	FROM MOBILE POWER DISTRIBUTION UNIT
9	SOILED CART LIFT	MOBILE SPS MANUFACTURER	CONTRACTOR	MOBILE SPS MANUFACTURER	FROM MOBILE POWER DISTRIBUTION UNIT

NOTE:

1. THE ABOVE LEGEND AND SCHEDULE IS TYPICAL FOR AN INSTALLATION OF THIS TYPE. THE CONTRACTOR SHALL BE RESPONSIBLE FOR COORDINATING ALL CONTRACT REQUIREMENTS WITH THE TEMPORARY MOBILE SPS MANUFACTURER. SHOULD THE TEMPORARY MOBILE SPS MANUFACTURER NOT PROVIDE ONE OF THE FOLLOWING IN THE LEGEND AND SCHEDULE ABOVE, IT SHALL BECOME THE RESPONSIBILITY OF THE CONTRACTOR TO PROVIDE THE MISSING MATERIAL AND LABOR. THE VA IS NOT RESPONSIBLE FOR ANY PURCHASING OF EQUIPMENT AND HOURS TO THE TEMPORARY EQUIPMENT. ALL CONNECTIONS TO EXISTING FACILITY UTILITIES SHALL BE COORDINATED WITH THE COR.

DOOR SCHEDULE									
DOOR TAG	WIDTH	HEIGHT	THICKNESS	TYPE	DOOR MATERIAL	DOOR FINISH	FRAME TYPE	FRAME MATERIAL	FRAME FINISH
1	3'-6"	7'-0"	1-3/4"	1	METAL	MANUF.	F1	H.M.	MANUF.
2	3'-6"	7'-0"	1-3/4"	1	METAL	MANUF.	F1	H.M.	MANUF.
3	3'-6"	7'-0"	1-3/4"	1	METAL	MANUF.	F1	H.M.	MANUF.
4	3'-0"	7'-0"	1-3/4"	1	METAL	MANUF.	F1	H.M.	MANUF.
5	3'-0"	7'-0"	1-3/4"	1	METAL	MANUF.	F1	H.M.	MANUF.
6	3'-6"	7'-0"	1-3/4"	1	ALUM.	MANUF.	F1	H.M.	MANUF.

1. SISING SHALL BE AS SHOWN ON PLANS.

2. DOORS AND FRAMES SHALL BE CONSTRUCTED WITH SEAMLESS CONSTRUCTION AND NO RECESSES AT TOP AND BOTTOM EDGES.

3. DOORS SHALL BE SOLID OR COMPLETED FOAM FILLED.

4. GLAZING IN GLAZING FRAMES SHALL BE FULLY SEALED.

FINISH SCHEDULE												
LOCATION		FLOORS		INTERIOR WALLS		CEILING		EXTERIOR WALLS		ROOF		REMARKS
ROOM NAME	MATERIAL	FINISH	BASE	MATERIAL	FINISH	MATERIAL	FINISH	MATERIAL	FINISH	MATERIAL	FINISH	
TEMPORARY ENCLOSURE (SLAM OR GROUND)	PLY/STYRING CONCRETE	F-2	F-2 (S&T) INTEGRAL COVE (BASE)	GYPSUM	P-1	GIP	P-1	WOOD	P-4	WOOD	ASPHALT SHINGLE	ATTACH FLOORING WITH MOISTURE/CURB-18 ENHANCED ADHESIVE, MECHANICALLY ANCHOR TO RATCH. WATER DRAIN & COMPLETE.
TEMPORARY ENCLOSURE (ACCESS CORRIDOR)	WOOD (BASED) CONCRETE	F-3	RB-1 (S&T) INTEGRAL COVE)	GYPSUM	P-1	GIP	P-1	WOOD	P-4	WOOD	ASPHALT SHINGLE	

Site Utility Requirements

Power
480V, 3PH, 60Hz, 700A MOP

Supply Water
Municipal (US EPA Potable)
Cold - 60 GPM

Waste Water
4" Dia. Site Connection
40-60 psi Dynamic

Revisions:	Date:

CONSULTANT

ENGINEER OF RECORD

FELENER

FE PROJECT #: 19-263
22 Hubbard St., Suite 2A,
Madisonville, KY 40340
1-800-343-1881 or 502-343-8996

181 Church St., Suite 100,
Poughkeepsie, NY 12601
1-800-654-0774 or 845-220-8775

UNAUTHORIZED ALTERATION OR ADDITION TO A PLAN BEARING A LICENSED PROFESSIONAL ENGINEER'S SEAL IS A VIOLATION OF STATE EDUCATION LAW.



Office of Construction and Facilities Management

VA U.S. Department of Veterans Affairs

Drawing Title
ARCHITECTURAL: SITE PLAN

Approved: Project Director

Phase
100% FOR CONSTRUCTION

Project Title
VA SYRACUSE REPAIR SPS DEFICIENCIES

Location
VAMC, SYRACUSE, NY

Issue Date
02-21-2025

Checked
EDF


Drawn
SRB

Project Number
528A7-19-720

Building Number
1

Drawing Number
AS-002

PAGE: 9 of 99

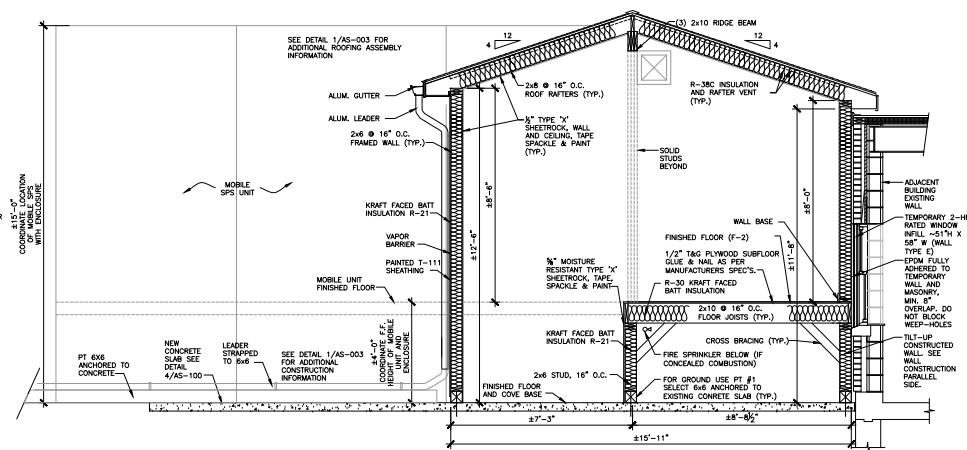


2 POST CLEAN LIFT SECTION
SCALE: 1/2"=1'-0"

6#6 P.T. CONC. WOOD
SILL W/ 1" WEDGE
ANCHOR BOLTS 72"
O.C. MAX., 12" MAX.
FROM CORNERS (TYP.)

FLASHING (TYP.)


SILL GASKET, GROUT,
BACKER BOARD, SEALANT
AND ANY MATERIAL
REQUIRED TO PROVIDE
WEATHER TIGHT SEAL
BETWEEN CONCRETE
AND PT WOOD (TYP.)

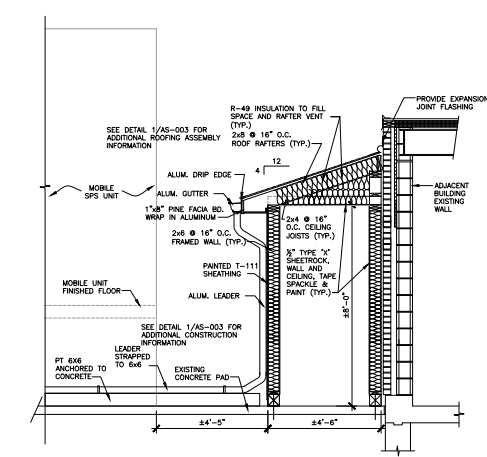

5 CORRIDOR SECTION
SCALE: 1/2"=1'-0"

Project Title VA SYRACUSE REPAIR SPS DEFICIENCIES		Project Number 528A7-19-720	
Location VAMC, SYRACUSE, NY		Building Number 1	
Issue Date 02-21-2025	Checked EDF	Drawn SRB	AS-003

PAGE: 10 OF 90

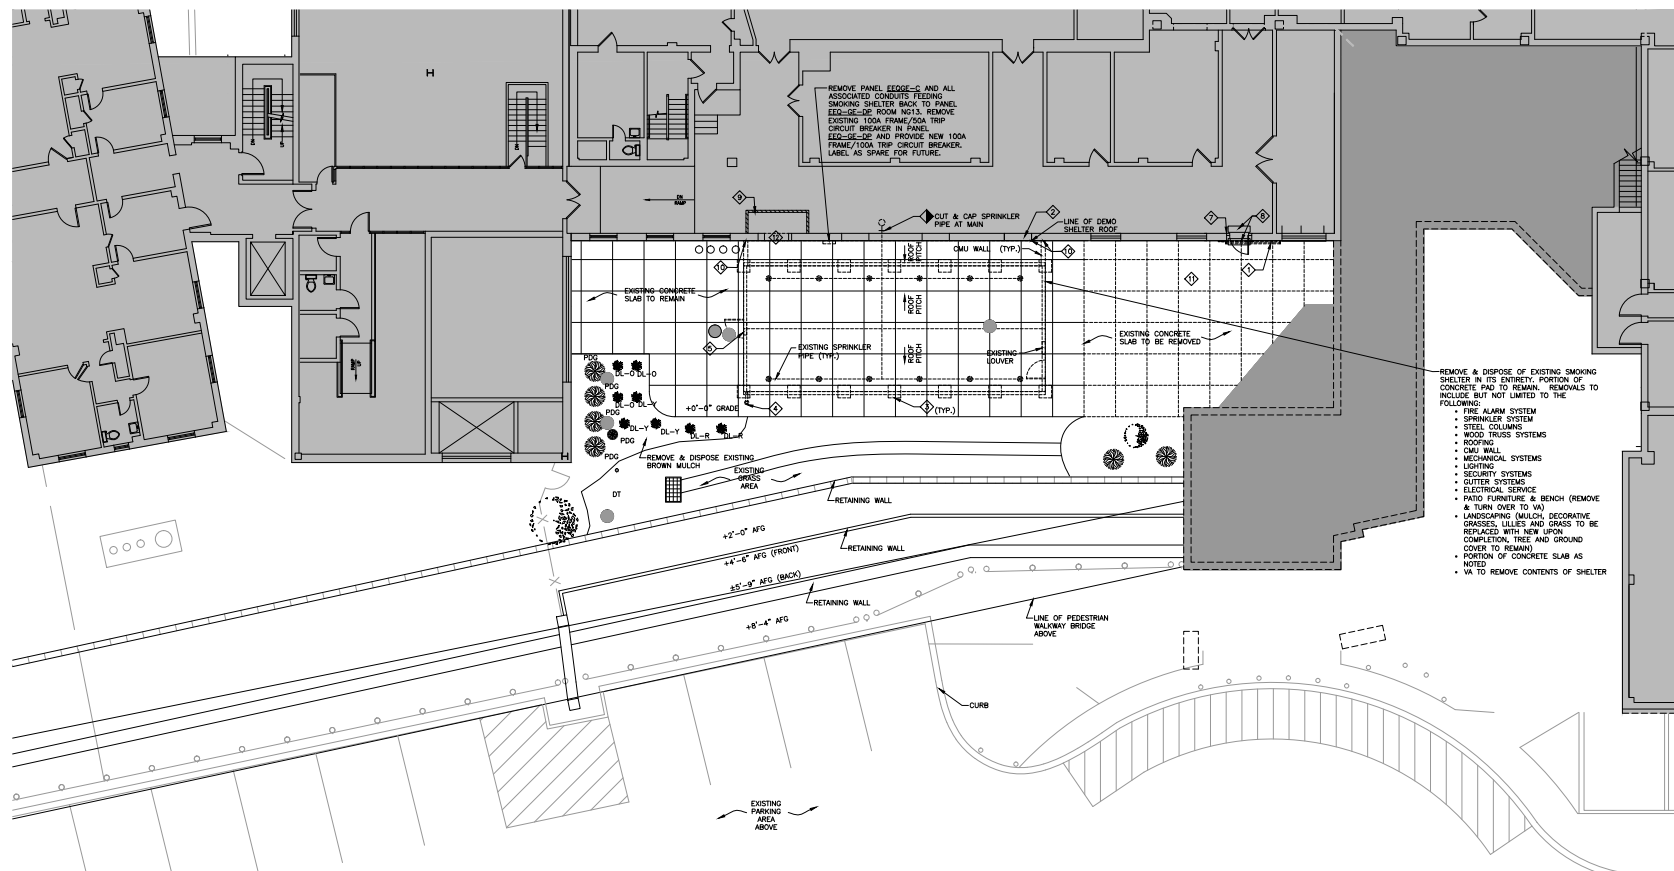

FLOOR PLAN LEGEND

	EXISTING AREA TO REMAIN (NOT IN SCOPE)
	AREA IN SCOPE
	EXISTING WALL TO REMAIN
	EXISTING DOOR TO REMAIN
	EXISTING CASEWORK TO REMAIN
	EXISTING WALL TO BE REMOVED
	EXISTING DOOR TO BE REMOVED
	EXISTING CASEWORK/CONCRETE TO BE REMOVED

KEYED NOTE:

- ▶ REMOVE AND DISPOSE EXISTING SLUING DOOR & PREPARE SURFACE FOR INSTALLATION OF NEW SLUING DOOR CONFORMING TO NEW YORK.
- ▶ REMOVE AND RESTORE FOR RE-INSTALLATION EXISTING ROOF TOP PARAPET RAILINGS.
- ▶ REMOVE AND DISPOSE EXISTING STAIRS AND REPLACE WITH CONCRETE SLAB AREA (TYP.)
- ▶ REMOVE GLASS & DOWNSPOUT AND COVER OVER STORM DRAIN OPENING (TYP.)
- ▶ REMOVE AND DISPOSE EXISTING EXHAUST FAN AND ALL ITS APPURTENANCES.
- ▶ NOT USED.
- ▶ GUN BARRIER, MIN. WIDTH 4'-0", PROVIDE AIR CURTAIN MONITORS AS REQUIRED.
- ▶ PROVIDE WALK-OFF (TACKY) MAT.
- ▶ TEMPORARY PARTITION CHAIR WALL, 2-A.
- ▶ REPAIR AND REPOINT EXISTING EXTERIOR MASONRY WALL FINISHES TO REMAIN TO MATCH EXISTING.
- ▶ REMOVE PORTION OF EXISTING 4" THICK CONCRETE ON CHAIR WALL, 2-A, 1'-0" TO 5'-0" AREA. PREPARE FOR INSTALLATION OF NEW BRICK GROUND AND 4" THICK CONCRETE IN SAME AREA.
- ▶ REMOVE PORTION OF MASONRY EXTERIOR WALL AND STAIR DOOR DOOR FRAME TO EXPOSE EXISTING AREA PREVIOUSLY IN-AS/REPAIRED WHERE WINDOW WAS LOCATED. SEE DRAWING FOR WINDOW AS-100 AND DETAILS 1.2, AS/AS-401 FOR WINDOW REPAIR.

1 ARCHITECTURAL: SMOKING SHELTER DEMOLITION PLAN
SCALE: 1/8"=1'-0"

PLANTING SCHEDULE

PLANTING SCHEDULE				
SYMBOL	ABBREVIATION	NAME	SIZE	REMARK
	DT	DECIDUOUS TREE	8"-10" HEIGHT	EXISTING TO REMAIN, DO NOT DISTURB
	PDG	PERENNIAL DECORATIVE GRASS		BURLAP & BALL
	DL	DAY LILY	5 GALLON CONTAINER	O-ORANGE R-RED Y-YELLOW

PROJECT NOTES:

1. CONTRACTOR SHALL REMOVE AND STORE ALL VA PROPERTY AS SPECIFIED IN THESE DOCUMENTS AND RESTORE IT BACK TO WORKING CONDITION AS SHOWN ON THE DRAWINGS. CONTRACTOR SHALL PROVIDE A WELL-CONDITIONED, SAFE STORAGE SPACE FOR THE VA EQUIPMENT THAT IS TO BE RE-INSTALLED. THE STORAGE SHALL NOT BE ON VA PROPERTY AND IT IS THE CONTRACTORS RESPONSIBILITY TO MOVE THE VA ITEMS FROM THE VAMC FACILITY TO THE STORAGE SPACE AND BACK TO THE VAMC WHEN RE-INSTALLATION IS REQUIRED. THE CONTRACTOR IS RESPONSIBLE FOR ALL DAMAGE TO VA ITEMS INCURRED DURING REMOVAL, TRANSPORT AND RE-INSTALLATION.
2. ALL PENETRATIONS THROUGH MASONRY WALL, REMOVED DURING CONSTRUCTION, TO BE PATCHED, INTERIOR AND EXTERIOR, WITH MATERIALS TO MATCH EXISTING AND SHALL PROVIDE REQUIRED FIRE RATING.

[illegible]

CONSULTANT

ENGINEER OF RECORD


FELLENZER
ENGINEERING LLP

FE PROJECT #: 19-263 www.felp.com

22 Mulberry St., Suite 2A,
Middletown, NY 10940
1-845-343-1811 or 1-845-343-4566

181 Church St., Suite 100
Poughkeepsie, NY 12601
1-845-544-8701 or 1-855-320-8733

UNAUTHORIZED ALTERATION OR ADDITION TO A PLAN
BEARING A LICENSED PROFESSIONAL ENGINEER'S SEAL
IS A VIOLATION OF STATE ENGINEERING LAW.

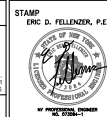

Office of
Construction
and Facilities
Management

 U.S. Department
of Veterans Affairs

Drawing Title

ARCHITECTURAL:
SMOKE SHELTER DEMOLITION PLAN

Approved: Project Director

Phase	100% FOR CONSTRUCTION
-------	-----------------------

Project Title	VA SYRACUSE REPAIR SPS DEFICIENCIES
---------------	--

Location	VAMC SYRACUSE NY
----------	------------------

Issue Date
02-21-2025

Project Number	
----------------	--


528A7-19-720

Building Number	1
-----------------	---

	Drawing Number

AD-100
PAGE: 11 of 99

A
B
C
D
E
F

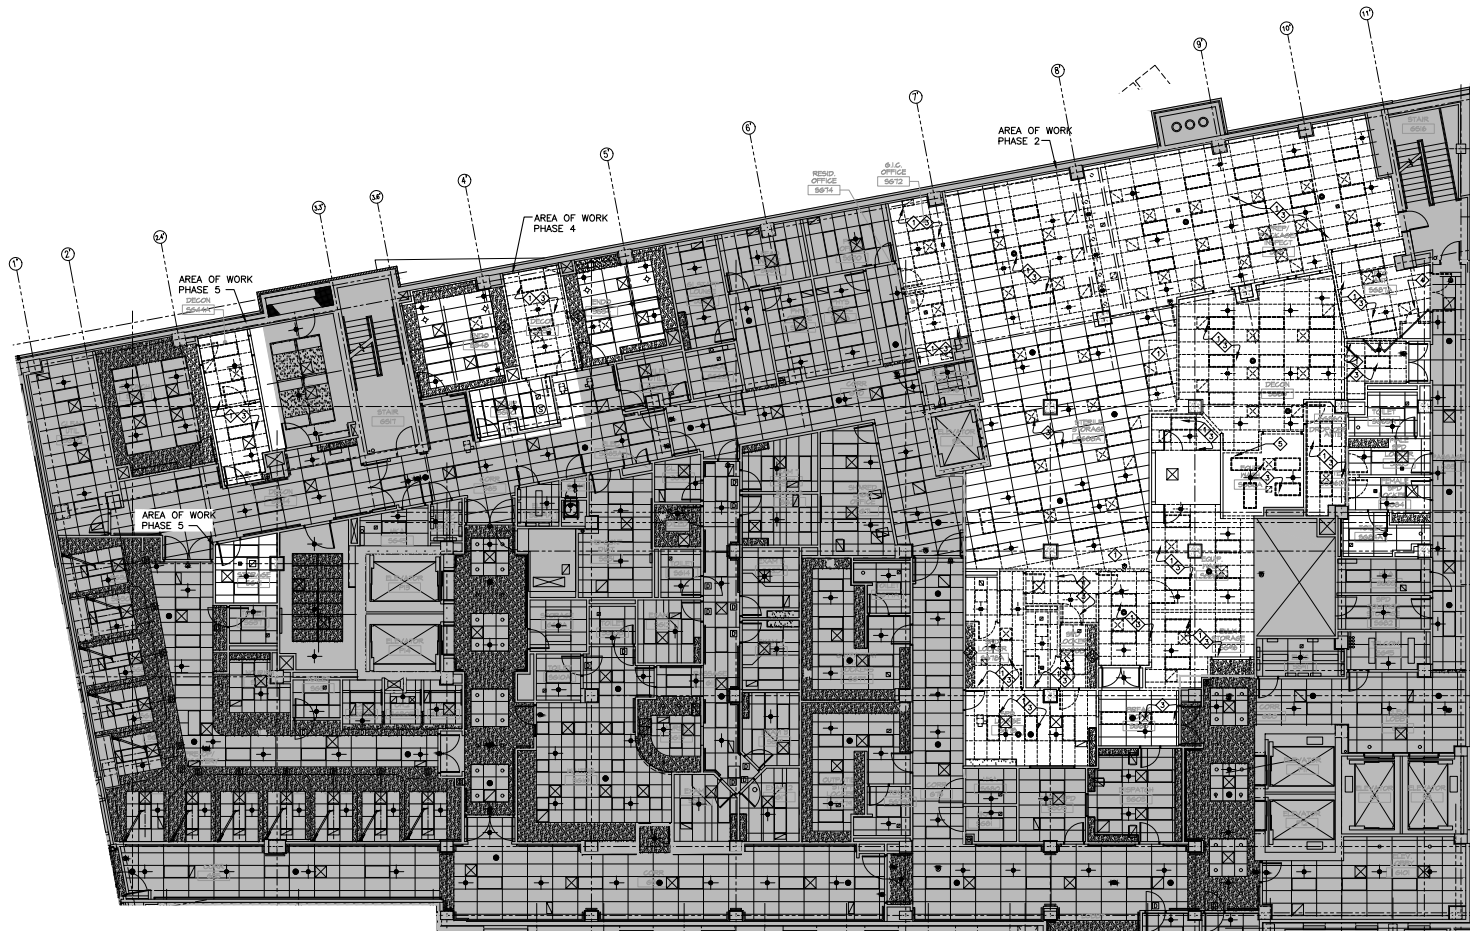

1 ARCHITECTURAL: DEMOLITION GROUND FLOOR REFLECTIVE CEILING PLAN
SCALE: 1/8"=1'-0"

- KEYED NOTE:
- EXISTING CEILING GRID AND TILE TO BE REMOVED AND DISPOSED. REPLACE WITH NEW. REFER TO CONSTRUCTION DRAWINGS FOR MORE INFORMATION.
 - EXISTING GYPSUM CEILING TO BE REMOVED AND DISPOSED. REPLACE WITH NEW. REFER TO CONSTRUCTION DRAWINGS FOR MORE INFORMATION.
 - EXISTING MECHANICAL, FIRE PROTECTION, AND ELECTRICAL DEVICES TO BE REMOVED AND DISPOSED. REFER TO MEP DEMOLITION DRAWINGS FOR MORE DETAILED INFORMATION.
 - EXISTING SPRINKLER HEAD NEXT TO THE RETURN GRILLE (NOT SHOWN).
 - EXISTING SMALL ACCESS PANEL LOCATED PLAN NORTH OF THIS LIGHT FIXTURE TO BE REMOVED (NOT SHOWN).

FLOOR PLAN LEGEND

- EXISTING AREA TO REMAIN (NOT IN SCOPE)
- AREA IN SCOPE
- EXISTING WALL TO REMAIN
- EXISTING DOOR TO REMAIN
- EXISTING CASEWORK TO REMAIN
- EXISTING WALL TO BE REMOVED
- EXISTING DOOR TO BE REMOVED

ROP LEGEND

- EXISTING GRID/CEILING TILE TO REMAIN
- EXISTING GYPSUM CEILING TO REMAIN
- EXISTING GRID/CEILING TILE TO BE REMOVED
- EXISTING GYPSUM CEILING TO BE REMOVED
- EXISTING SUPPLY TO REMAIN
- EXISTING RETURN TO REMAIN
- EXISTING EXHAUST TO REMAIN
- FIRE SPRINKLER HEAD TO REMAIN
- HVAC SUPPLY DIFFUSER TO BE REMOVED
- HVAC RETURN GRILLE TO BE REMOVED
- EXHAUST AIR TERMINAL TO BE REMOVED
- FIRE SPRINKLER HEAD TO BE REMOVED
- 2x2 LIGHT TO BE REMOVED
- 2x4 LIGHT TO BE REMOVED
- 2x2 ACCESS PANEL TO BE REMOVED
- 2x4 ACCESS PANEL TO BE REMOVED
- CEILING MOUNTED SPEAKER TO BE REMOVED
- CEILING MOUNTED EXIT SIGN TO BE REMOVED

Revisions:	Date:

CONSULTANT

ENGINEER OF RECORD
FELLENER
ENGINEERING LLP
PROJECT # 19-263
22 Mulberry St., Suite 2A, Madisonville, KY 40340 1.800.343.1481 or 502.343.4996
181 Church St., Suite 100, Poughkeepsie, NY 12601 1.800.654.8754 or 845.320.8755
www.fellp.com
UNAUTHORIZED ALTERATION OR ADDITION TO A PLAN BEARING A LICENSED PROFESSIONAL ENGINEER'S SEAL IS A VIOLATION OF STATE EDUCATION LAW.


STAMP
ERIC D. FELLENER, P.E.

Office of Construction and Facilities Management

Drawing Title
ARCHITECTURAL: DEMOLITION GROUND FLOOR REFLECTIVE CEILING PLAN
Approved: Project Director

Phase
100% FOR CONSTRUCTION

Project Title
VAMC SYRACUSE REPAIR SPS DEFICIENCIES
Location
VAMC, SYRACUSE, NY
Issue Date
02-21-2025
Checked
EDF
Drawn
SRB
Project Number
528A7-19-720
Building Number
1
Drawing Number
AD-102
PAGE: 13 OF 99

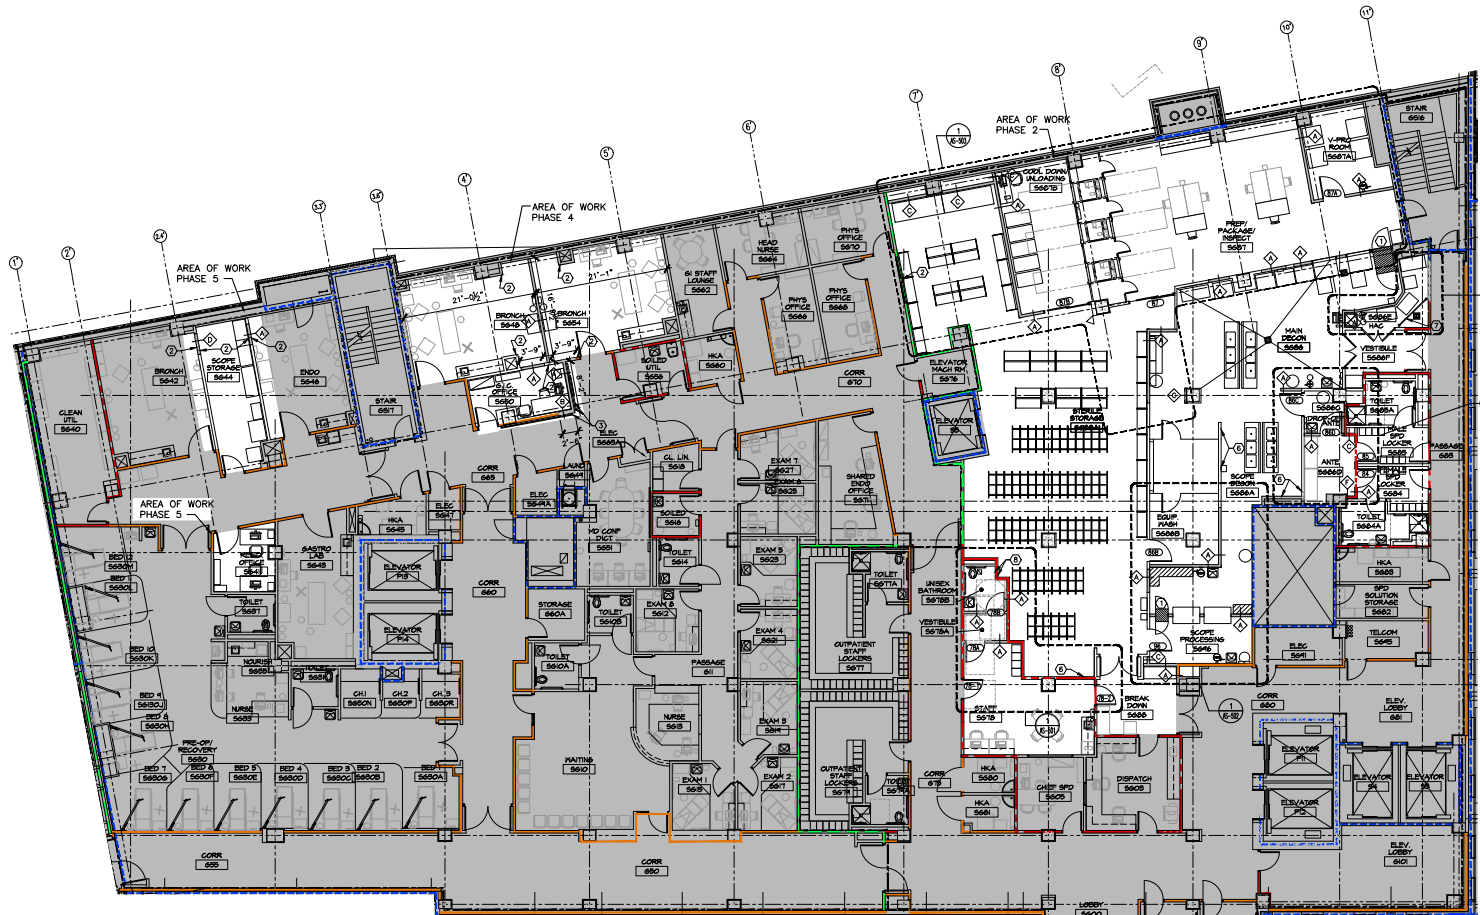

1 ARCHITECTURAL: NEW GROUND FLOOR PLAN
SCALE: 1/8"=1'-0"

- KEYED NOTES:**
- PROVIDE PASS-THROUGH CHAMBER. CHAMBER SHALL BE NEWLY FRAMED INTO THE WALL PER THE MANUFACTURER'S INSTRUCTIONS. ALL HOLES AND IMPERFECTIONS IN THE WALLS SHALL BE REPLACED AND FINISHED/PAINTED TO MATCH EXISTING. SEE DETAIL 2/AS-701 AND 1/AS-701.
 - PATCH, PRIME & PAINT WALL AREA TO MATCH SURROUNDINGS WHERE EXISTING WALL WAS REMOVED FOR FLUSH AND SMOOTH SURFACE. REFER TO FINISH SCHEDULE FOR FINAL WALL FINISH.
 - EXISTING HANDRAIL TO BE CLEANED & REINSTALLED IN NEW LOCATION AS SHOWN.
 - REMOVE & INSTALL NEW 11'-0" LONG HANDRAIL TO MATCH EXISTING COLOR & STYLE. SEE DETAIL.
 - PREPARE EXISTING FLOOR FOR NEW FLOORING PER MANUFACTURER'S RECOMMENDATIONS AND SPECIFICATIONS.
 - PROVIDE NEW GYPSUM ON WALLS OF REMOVED WALL TILE.
 - PROVIDE NEW HEAVY DUTY SAFETY RAIL, 3/4" 42" HIGH STEEL PIPE FRAME WITH 1/2" RAIL. PROVIDE SINGLE SOCKET FLOOR MOUNT BASE. RAILS TO HAVE LONG LASTING SAFETY YELLOW FINISH.
 - PROVIDE 1/2" FIRE RATED GYPSUM, MOISTURE RESISTANT ON WEST SIDE, TO PROVIDE 1 HR FIRE RATING.
- NOTES:**
- NEW WALL CONSTRUCTION IS PROPOSED FROM FLOOR TO UNDERSIDE OF DECK FOR NOISE CONTROL.
 - COORDINATE OPENINGS IN NEW WALL WITH THE DUCT/Pipe/PIPE/PRIVILEGE & ELECTRICAL WIRING.
 - CONSOLIDATE OPENINGS ABOVE THE CEILING WHEN POSSIBLE/PRACTICAL.
 - AT DOOR AREAS, INFILL UP TO UNTEL WITH JACK STUDS ON EACH SIDE. SPACE STUDS @ 14" O.C. OFFSET AT CENTER POINT.
 - PHASE 3 HAS INCLUDE MOBILE SPS INSULATION AND REMOVAL. SEE DRAWINGS G-004 FOR COMPLETE PHASING PLAN.
- LIFE SAFETY LEGEND:**
- SMOKE BARRIER - 1 HR FIRE RATED
 - CORRIDOR WALL - SMOKE PARTITION - 0 HR FIRE RATED (LIMIT TRANSFER OF SMOKE)
 - 1 HR FIRE RATED BARRIER (45 MINUTE DOORS)
 - 2 HR FIRE RATED BARRIER (1-1/2 HR DOOR AND FIRE DAMPERS)
- FLOOR PLAN LEGEND:**
- EXISTING AREA TO REMAIN (NOT IN SCOPE)
 - AREA IN SCOPE
 - EXISTING WALL TO REMAIN
 - EXISTING DOOR TO REMAIN
 - EXISTING CASEWORK TO REMAIN
 - NEW WALL
 - NEW DOOR
 - NEW CASEWORK/CONCRETE
- PLUMBING FIXTURES TO REMAIN**
- FEC FIRE EXTINGUISHER CABINET
 - FHC FIRE HOSE CABINET
 - ZV ZONE VALVE BOX, COORDINATE WITH PLUMBING DWGS
 - AP MED GAS ALARM PANEL, COORDINATE WITH PLUMBING DWGS
 - PP ELECTRICAL PANEL, COORDINATE WITH ELECTRICAL DWGS
 - CG CORNER GUARD
- NEW PLUMBING FIXTURES**
- FEC FIRE EXTINGUISHER CABINET
 - FHC FIRE HOSE CABINET
 - ZV ZONE VALVE BOX, COORDINATE WITH PLUMBING DWGS
 - AP MED GAS ALARM PANEL, COORDINATE WITH PLUMBING DWGS
 - PP ELECTRICAL PANEL, COORDINATE WITH ELECTRICAL DWGS
 - CG CORNER GUARD

Revisions:	Date:

CONSULTANT

ENGINEER OF RECORD
FELENER
ENGINEERING LLP
FE PROJECT #: 19-263
22 Mulberry St., Suite 2A, Madisonville, KY 40340 1-800-343-1881 N. 845-343-4995
181 Church St., Suite 100, Poughkeepsie, NY 12601 1-800-654-0754 N. 845-330-8775
www.feleneer.com
UNAUTHORIZED ALTERATION OR ADDITION TO A PLAN BEARING A LICENSED PROFESSIONAL ENGINEER'S SEAL IS A VIOLATION OF STATE EDUCATION LAW.


STAMP
ERIC D. FELENER, P.E.

Office of Construction and Facilities Management
VA U.S. Department of Veterans Affairs

Drawing Title
ARCHITECTURAL: NEW GROUND FLOOR PLAN
Approved: Project Director

Phase
100% FOR CONSTRUCTION

Project Title
VA SYRACUSE REPAIR SPS DEFICIENCIES
Location
VAMC, SYRACUSE, NY
Issue Date
02-21-2025
Checked
EDF
Drawn
SRB
Project Number
528A7-19-720
Building Number
1
Drawing Number
AS-101
PAGE: 15 OF 99

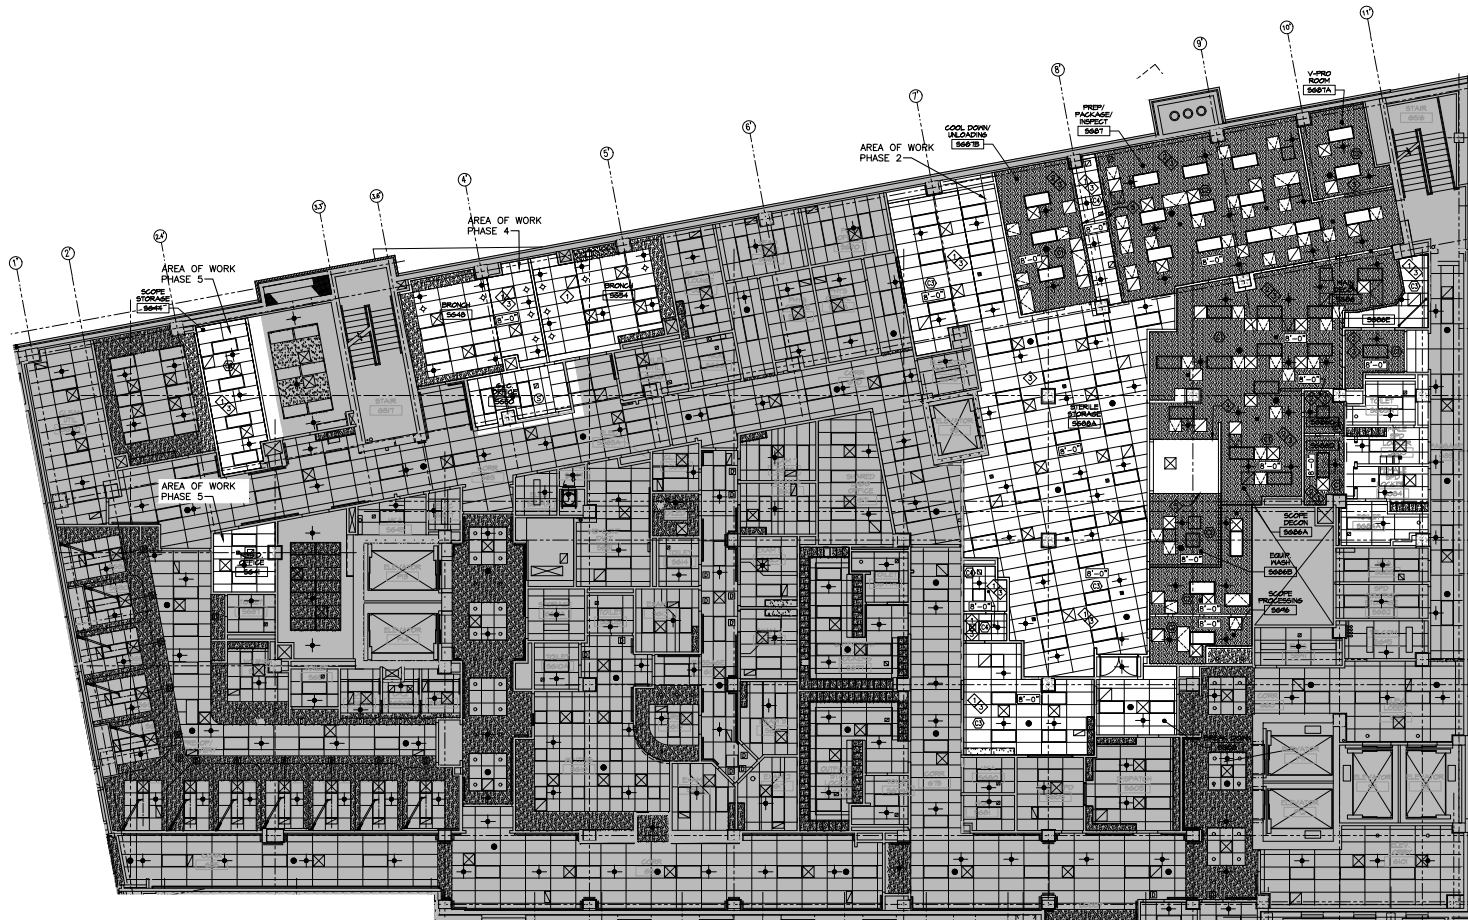

1 ARCHITECTURAL: NEW GROUND FLOOR REFLECTIVE CEILING PLAN
SCALE: 1/8"=1'-0"

- LEGEND:**
- ① SUSPENDED GYPSUM WALLBOARD GRID SYSTEM CEILING WITH DRY-DROP CEILING FINISH (P-1).
 - ② SUSPENDED GYPSUM WALLBOARD GRID SYSTEM CEILING WITH URETHANE HIGH BUILD GLAZE (SPECIAL COATING) FINISH (P-2).
 - ③ 2x4 DROP CEILING, SEE DETAILS 6&7/AS-701. HEIGHT TO MATCH EXISTING.
 - ④ 2x2 DROP CEILING, SEE DETAILS 6&7/AS-701. HEIGHT INDICATED ON PLANS.
 - ⑤ GYPSUM WALLBOARD SOFFIT SYSTEM CEILING OVER LOCKER AREA. HEIGHT TO MATCH EXISTING, 6'-0"± V.I.F.

- KEYED NOTE:**
- ◇ NEW CEILING GRID AND TILE, HEIGHTS AS INDICATED.
 - ◇ NEW GYPSUM CEILING, HEIGHTS AS INDICATED.
 - ◇ NEW MECHANICAL, FIRE PROTECTION, AND ELECTRICAL DEVICES TO BE INSTALLED. REFER TO MEP CONSTRUCTION DRAWINGS FOR MORE DETAILED INFORMATION.
 - ◇ EXTENT OF C1 CEILING (INTERIOR FACE OF ROOM)
 - ◇ EXTENT OF C2 CEILING (INTERIOR FACE OF ROOM)

- GENERAL NOTES:**
- COORDINATE CEILING ACCESS PANELS WITH SUSPENDED GRID SYSTEM.

FLOOR PLAN LEGEND

- EXISTING AREA TO REMAIN (NOT IN SCOPE)
- AREA IN SCOPE
- EXISTING WALL TO REMAIN
- EXISTING DOOR TO REMAIN
- EXISTING CASEWORK TO REMAIN
- NEW WALL
- NEW DOOR

RCP LEGEND

- EXISTING GRID/CEILING TILE TO REMAIN
- EXISTING GYPSUM CEILING TO REMAIN
- NEW GRID/2'x4' CEILING TILE
- NEW GYPSUM CEILING
- EXISTING SUPPLY TO REMAIN
- EXISTING RETURN TO REMAIN
- EXISTING EXHAUST TO REMAIN
- FIRE SPRINKLER HEAD TO REMAIN
- NEW HVAC SUPPLY DIFFUSER
- NEW HVAC RETURN GRILLE
- NEW EXHAUST AIR TERMINAL
- NEW FIRE SPRINKLER HEAD
- NEW 2x2 LIGHTING FIXTURE
- NEW 2x4 LIGHTING FIXTURE
- NEW 2x2 ACCESS PANEL
- NEW 2x4 ACCESS PANEL
- NEW CEILING MOUNTED SPEAKER
- NEW CEILING MOUNTED EXIT SIGN

Revisions:	Date:

CONSULTANT

ENGINEER OF RECORD

FELENER
ENGINEERING LLP

FE PROJECT #: 19-263
22140berry St., Suite 2A,
Madisonville, KY 40340
1.800.343-1481 / 502.343-4996

181 Church St., Suite 100,
Poughkeepsie, NY 12601
1.800.654-8754 / 845.320-8755

UNAUTHORIZED ALTERATION OR ADDITION TO A PLAN
BEARING A LICENSED PROFESSIONAL ENGINEER'S SEAL
IS A VIOLATION OF STATE EDUCATION LAW.

STAMP
ERIC D. FELENER, P.E.



Office of
Construction and
Facilities
Management

VA U.S. Department of
Veterans Affairs

Drawing Title
ARCHITECTURAL:
NEW GROUND FLOOR REFLECTIVE
CEILING PLAN

Approved: Project Director

Phase
100% FOR
CONSTRUCTION

Project Title
VA SYRACUSE
REPAIR SPS DEFICIENCIES

Location
VAMC, SYRACUSE, NY

Issue Date
02-21-2025

Checked
EDF

Drawn
SRB

Project Number
528A7-19-720

Building Number
1

Drawing Number
AS-201

PAGE: 16 OF 99



1 ARCHITECTURAL: GROUND FLOOR EQUIPMENT PLAN
SCALE: 1/8"=1'-0"

EXISTING REUSED EQUIPMENT LEGEND

- 1 WALL MOUNTED ELECTRIC WH
- 2 WM R.O. MEMBRANES & DRIP PAN
- 3 FLOOR MOUNTED BOOSTER PUMP
- 4 WALL MOUNTED CHEMICAL ALARM
- 5 WM R.O. MEMBRANES & DRIP PAN
- 6 FLOOR MOUNTED BOOSTER PUMP
- 7 WALL MOUNTED ELECTRIC WH
- 8 CHD FLR. NURSE CALL PANEL A
- 9 WALL MOUNTED CHEMICAL ALARM
- 10 NOT USED
- 11 WALL MOUNTED SCOPE BUDDY
- 12 TRIPLE BAY SINK/TABLE
- 13 WALL MOUNTED SINK
- 14 PASS THROUGH STERILIZER
- 15 PASS THROUGH STERILIZER
- 16 PASS THROUGH STERILIZER
- 17 CABINETS W/COUNTER TOP
- 18 CABINETS
- 19 LARGE SCALE STORAGE CASE
- 20 OLYMPIC CABINET DRYER
- 21 LARGE SCALE WASHER
- 22 LARGE SCALE WASHER
- 23 TWO (2) TABLE WORK STATION
- 24 TWO (2) TABLE WORK STATION
- 25 V-PRO STERILIZER
- 26 V-PRO STERILIZER
- 27 V-PRO STERILIZER
- 28 LARGE SCALE CART WASH
- 29 ULTRA SONIC CLEANER
- 30 ULTRA SONIC CLEANER
- 31 WALL MOUNTED CHEMICAL ALARM
- 32 ULTRA SONIC CLEANER
- 33 ULTRA SONIC CLEANER
- 34 NOT USED
- 35 NOT USED
- 36 WALL MOUNTED DISINFECTOR
- 37 WALL MOUNTED DISINFECTOR
- 38 WORK TABLE
- 39 TRITON DA VINCI WASHER
- 40 WALL MOUNTED TEMPERATURE SENSOR
- 41 WALL MOUNTED CHEMICAL ALARM
- 42 WALL MOUNTED MONITOR
- 43 STAINLESS PANELS AND DOORS
- 44 STAINLESS PANELS AND DOORS
- 45 STAINLESS PANELS AND DOORS
- 46 STAINLESS PANELS AND DOORS
- 47 CABINETS
- 48 COMPUTER WORKSTATION
- 49 COMPUTER WORKSTATION
- 50 MOVABLE STORAGE
- 51 OFFICE FURNITURE
- 52 COMPUTER & PRINTER
- 53 SCOPE STORAGE CABINET
- 54 SCOPE STORAGE CABINET
- 55 MOVABLE STORAGE
- 56 MOVABLE STORAGE
- 57 STORAGE RACK
- 58 MOVABLE EQUIPMENT
- 59 BENCH
- 60 LOCKERS
- 61 LOCKERS


PROVIDED NEW EQUIPMENT LEGEND

- 1 12"x30" TRIPLE BAY SINK [VC]
- 2 WALL MOUNTED SCOPE BUDDY [CC]
- 3 96"x30" TRIPLE BAY SINK/TABLE [VC]
- 4 24"x24"x24" PASS THROUGH CHAMBER (PC-1) [CC]
- 5 36"x48"x36" PASS THROUGH CHAMBER (PC-2) [CC]
- 6 48"x18" BENCH [CC]
- 7 PLUMBING FIXTURES (P-103, P-418 & P-516) [CC]
- 8 EMERGENCY EYE WASH / SHOWER UNIT (P-707) [CC]
- 9 EMERGENCY EYE WASH UNIT (P-708) [CC]
- 10 WASTE RECEPTACLE [VC]
- 11 COMPUTER & SS COUNTERTOP [VC]
- 12 WALL MOUNT COMPUTER [CC]
- 13 BARCODE SCANNER [VC]
- 14 SS WALL HUNG CABINET [CC]
- 15 THROUGH WALL MENDATOR [VC]
- 16 STORAGE RACKS [VC]
- 17 4" SHELF [CC]
- 18 MOP SINK [CC] (P-502)
- 19 PASS THROUGH STERILIZER
- 20 PASS THROUGH STERILIZER
- 21 PASS THROUGH STERILIZER
- 22 LOCKERS


ACQUISITION CODE LEGEND:
[CC] - CONTRACTOR FURNISHED AND INSTALLED
[VC] - VA FURNISHED, CONTRACTOR INSTALLED
[V] - VA FURNISHED AND INSTALLED

Revisions:		CONSULTANT	ENGINEER OF RECORD FELLENER ENGINEERING LLP FE PROJECT #: 19-263 22 Mulberry St., Suite 2A, Madison, NY 13093 1.845.343.1481 to 1.845.343.4999 UNAUTHORIZED ALTERATION OR ADDITION TO A PLAN BEARING A LICENSED PROFESSIONAL ENGINEER'S SEAL IS A VIOLATION OF STATE EDUCATION LAW.	STAMP ERIC D. FELLENER, P.E. 181 Church St., Suite 100, Poughkeepsie, NY 12601 1.845.454.8754 to 1.855.323.8770 NY PROFESSIONAL ENGINEER EXPIRES 12/31/2024	Office of Construction and Facilities Management VA U.S. Department of Veterans Affairs	Drawing Title ARCHITECTURAL: NEW GROUND FLOOR EQUIPMENT PLAN Approved: Project Director	Phase 100% FOR CONSTRUCTION	Project Title VA SYRACUSE REPAIR SPS DEFICIENCIES Location VAMC, SYRACUSE, NY Issue Date 02-21-2025 Checked EDF Drawn SRB	Project Number 528A7-19-720 Bidding Number 1 Drawing Number AS-301 PAGE: 17 OF 99
----------------------------------	--	-----------------------	--	---	---	--	---	---	--


File Name: F:\2019\10\20\SPS DEFICIENCY REPAIR, VA SYRACUSE\ARCHITECTURAL\10\AS-501 - AS-505.dwg (User: JAG) Date: Thu, 10/20/2022 1:17 PM

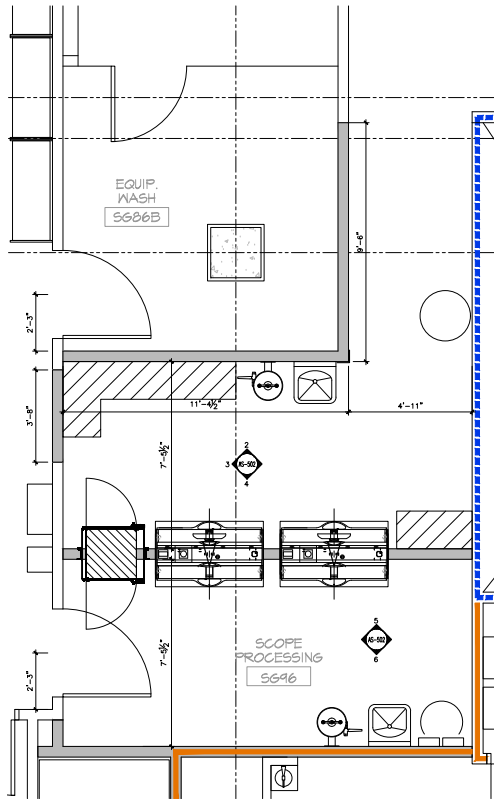


1 ENLARGED SCOPE PROCESSING SG96,
PORTION OF EQUIPMENT WASH SG86B
& PORTION OF SCOPE DECON-SG86A PLANS
SCALE: 1/2"=1'-0"

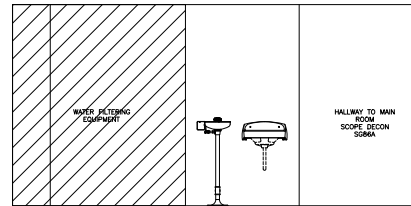


2 SCOPE DECON-SG86A - INTERIOR ELEVATION -W
SCALE: 1/2"=1'-0"

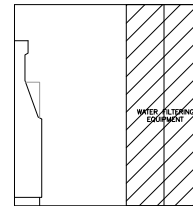


3 SCOPE DECON-SG86A - INTERIOR ELEVATION -S
SCALE: 1/2"=1'-0"

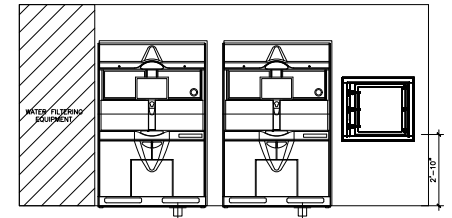

4 SCOPE DECON-SG86A - INTERIOR ELEVATION -E
SCALE: 1/2"=1'-0"

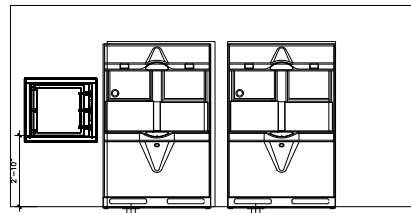

5 SCOPE PROCESSING-SG96- INTERIOR ELEVATION -W
SCALE: 1/2"=1'-0"

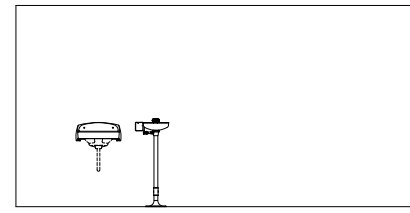

6 SCOPE PROCESSING-SG96- INTERIOR ELEVATION -E
SCALE: 1/2"=1'-0"


NOTES:

1. NEW WALL CONSTRUCTION IS PROPOSED FROM FLOOR TO UNDERSIDE OF DECK FOR NOISE CONTROL.
2. COORDINATE OPENINGS IN NEW WALL WITH THE DUCT/PIPE/SPRINKLER & ELECTRICAL WIRING.
3. CONSOLIDATE OPENINGS ABOVE THE CEILING WHEN POSSIBLE/PRACTICAL.
4. AT DOOR AREAS, INFILL UP TO LINTEL WITH JACK STUDS ON EACH SIDE. SPACE STUDS @ 16" O.C. OFFSET AT CENTER POINT.
5. PHASES 1&3 INCLUDE MOBILE SPS INSTALLATION AND REMOVAL. SEE DRAWINGS G-504 FOR COMPLETE PHASING PLAN.

Revisions:	Date:

CONSULTANT

ENGINEER OF RECORD
FELENER
ENGINEERING LLP
FE PROJECT #: 19-263
22 Mulberry St., Suite 2A,
Madison, NY 12550
1-845-343-1481 N. 845-343-4995
181 Church St., Suite 100,
Poughkeepsie, NY 12601
1-845-654-8754 N. 845-330-8735
UNAUTHORIZED ALTERATION OR ADDITION TO A PLAN
BEARING A LICENSED PROFESSIONAL ENGINEER'S SEAL
IS A VIOLATION OF STATE EDUCATION LAW.

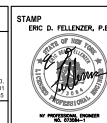


Office of
Construction
and Facilities
Management
VA U.S. Department
of Veterans Affairs

Drawing Title
ARCHITECTURAL:
ENLARGED FLOOR PLANS & ELEVATIONS
Approved: Project Director

Phase
100% FOR
CONSTRUCTION

Project Title VA SYRACUSE REPAIR SPS DEFICIENCIES	Project Number 528A7-19-720
Location VAMC, SYRACUSE, NY	Building Number 1
Issue Date 02-21-2025	Checked EDF
Drawn SRB	Drawing Number AS-502 PAGE: 20 OF 99

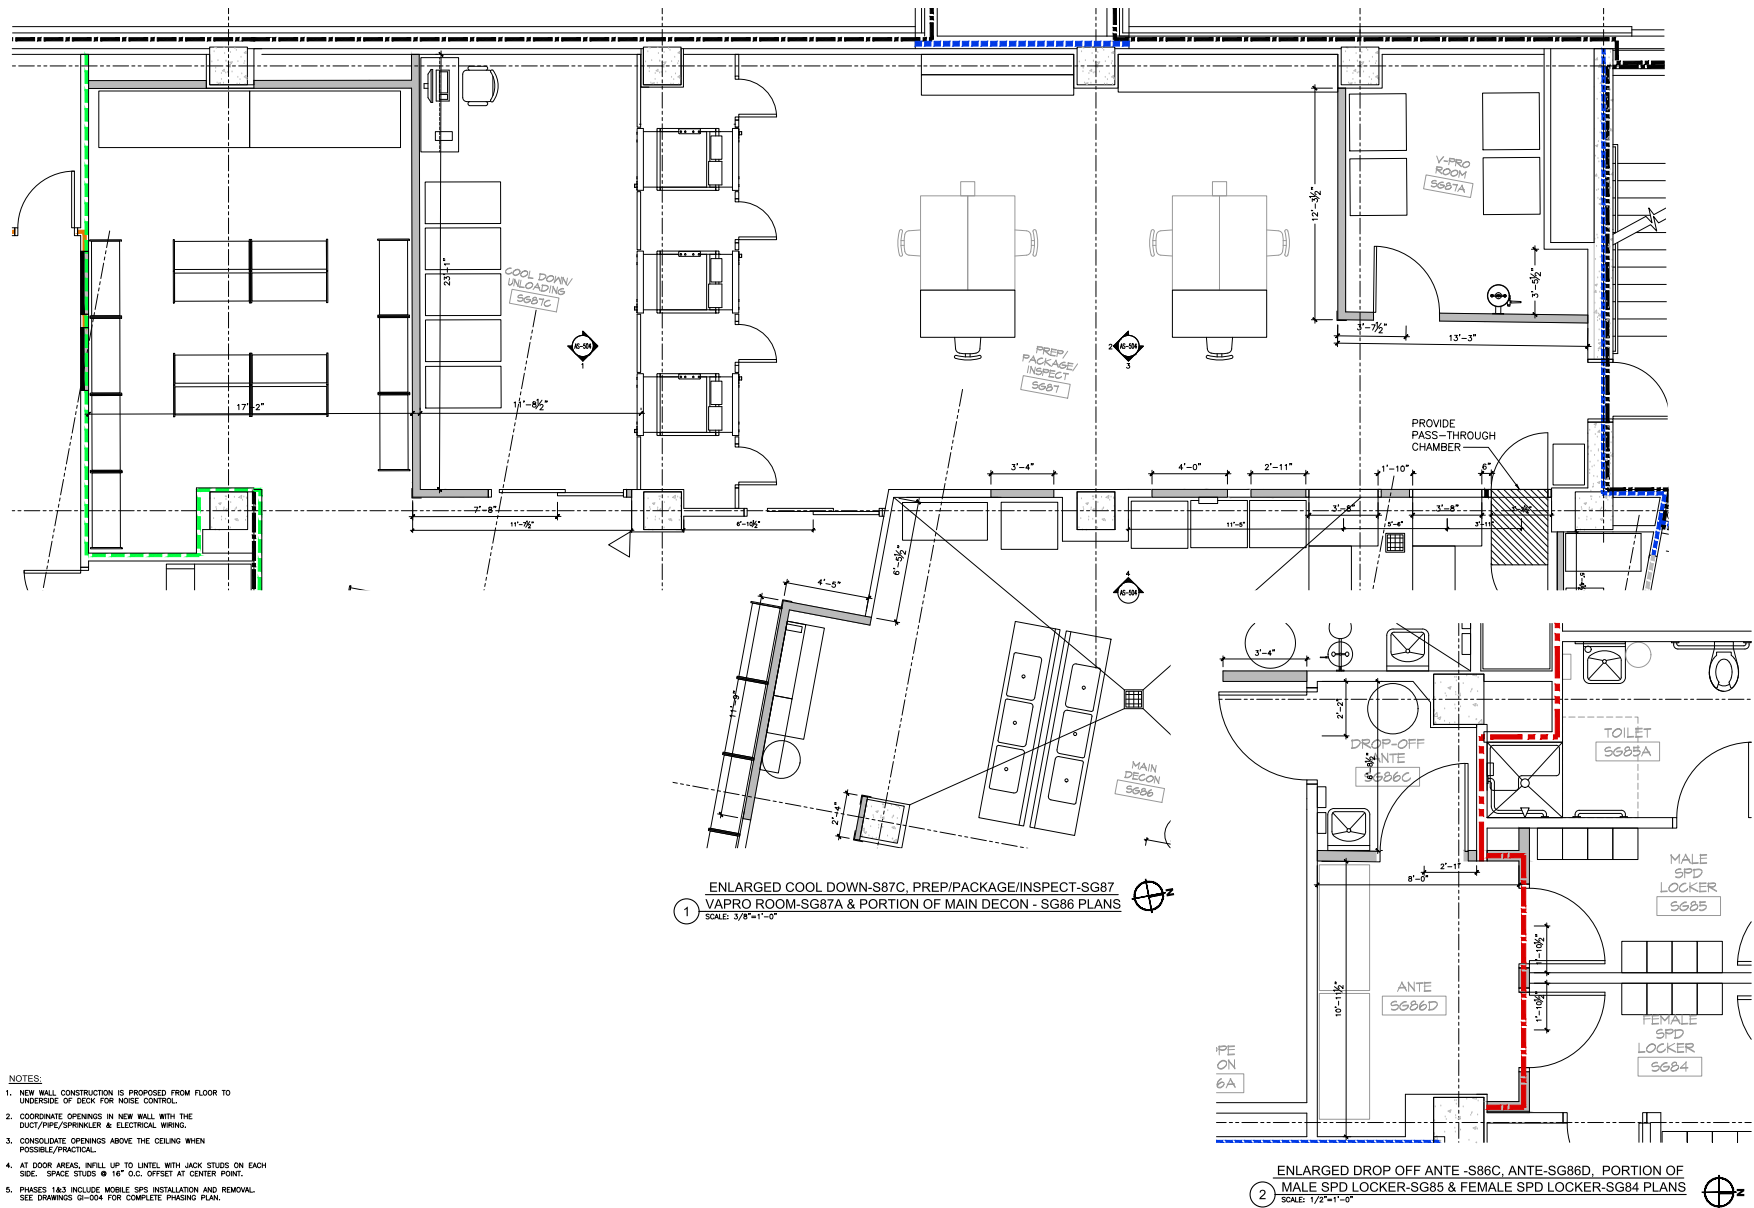

- NOTES:
1. NEW WALL CONSTRUCTION IS PROPOSED FROM FLOOR TO UNDERSIDE OF DECK FOR NOISE CONTROL.
 2. COORDINATE OPENINGS IN NEW WALL WITH THE DUCT/PIPE/SPRINKLER & ELECTRICAL WIRING.
 3. CONSOLIDATE OPENINGS ABOVE THE CEILING WHEN POSSIBLE/PRACTICAL.
 4. AT DOOR AREAS, INFILL UP TO LINTEL WITH JACK STUDS ON EACH SIDE. SPACE STUDS @ 14" O.C. OFFSET AT CENTER POINT.
 5. PHASES 1&3 INCLUDE MOBILE SPS INSTALLATION AND REMOVAL. SEE DRAWINGS G-004 FOR COMPLETE PHASING PLAN.

1 ENLARGED COOL DOWN-S87C, PREP/PACKAGE/INSPECT-SG87 VAPRO ROOM-SG87A & PORTION OF MAIN DECON - SG86 PLANS SCALE: 3/8"=1'-0"

2 ENLARGED DROP OFF ANTE-S86C, ANTE-SG86D, PORTION OF MALE SPD LOCKER-SG85 & FEMALE SPD LOCKER-SG84 PLANS SCALE: 1/2"=1'-0"

File Name: F:\2018\303 SPS DEFICIENCY REPAIR_VA SYRACUSE\ARCHITECTURAL\18-AS-501 - AS-505.dwg (User: JAG) Date: Thu, 04/01/2025, 1:11 PM

Revisions:	Date:

CONSULTANT

ENGINEER OF RECORD

FELLENER

ENGINEERING LLP

FE PROJECT #: 19-263

22 Mulberry St., Suite 2A, Middletown, NY 13560

1.845.343.1481 N. 845.343.4995

181 Church St., Suite 100, Poughkeepsie, NY 12601

1.845.654.8754 N. 855.335.8735

UNAUTHORIZED ALTERATION OR ADDITION TO A PLAN BEARING A LICENSED PROFESSIONAL ENGINEER'S SEAL IS A VIOLATION OF STATE EDUCATION LAW.

STAMP

ERIC D. FELLENER, P.E.

Professional Engineer Seal

Office of Construction and Facilities Management


VA U.S. Department of Veterans Affairs

Drawing Title
ARCHITECTURAL: ENLARGED FLOOR PLANS
Approved: Project Director


Phase
100% FOR CONSTRUCTION

Project Title
VA SYRACUSE REPAIR SPS DEFICIENCIES
Location
VAMC, SYRACUSE, NY
Issue Date
02-21-2025
Checked
EDF
Drawn
SRB


Project Number
528A7-19-720
Building Number
1
Drawing Number
AS-503
PAGE: 21 OF 99

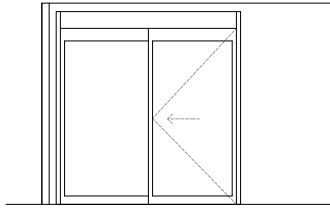


1 COOL DOWN/UNLOADING ROOM-SG87C INTERIOR ELEVATION -E
SCALE: 1/2"=1'-0"

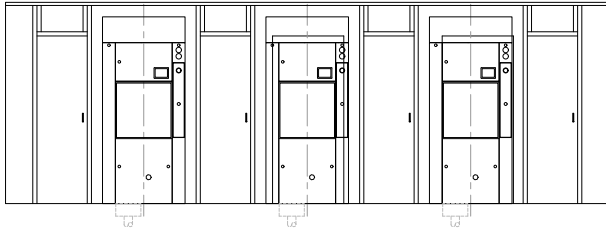

3 PREP/PACKAGE/INSPECT ROOM-SG87 INTERIOR ELEVATION -S
SCALE: 1/2"=1'-0"

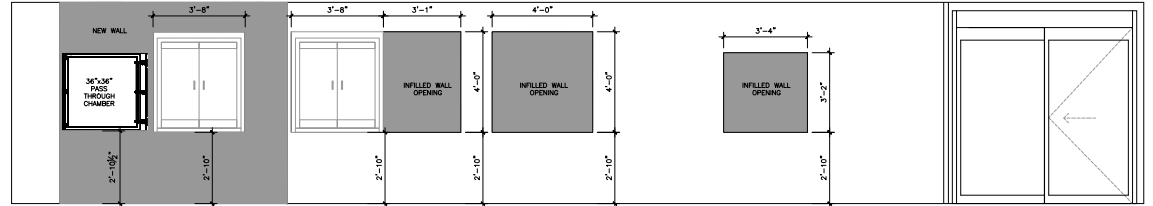

3 PREP/PACKAGE/INSPECT ROOM-SG87 INTERIOR ELEVATION -E
SCALE: 1/2"=1'-0"

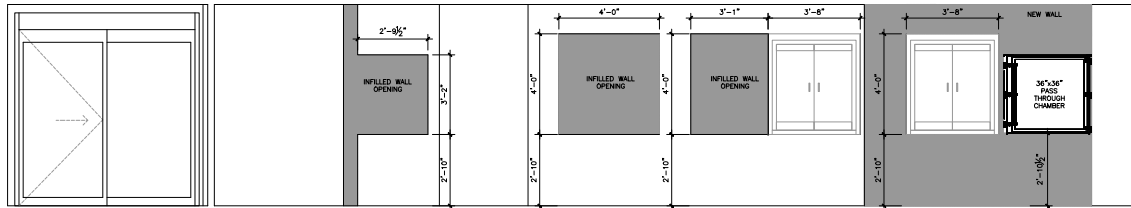


4 MAIN DECON ROOM-SG86 INTERIOR ELEVATION -W
SCALE: 1/2"=1'-0"

- NOTES:
1. NEW WALL CONSTRUCTION IS PROPOSED FROM FLOOR TO UNDERSIDE OF DECK FOR NOISE CONTROL.
 2. COORDINATE OPENINGS IN NEW WALL WITH THE DUCT/PWC/SPRINKLER & ELECTRICAL WIRING.
 3. CONSOLIDATE OPENINGS ABOVE THE CEILING WHEN POSSIBLE/PRACTICAL.
 4. AT DOOR AREAS, INFILL UP TO LINTEL WITH JACK STUDS ON EACH SIDE. SPACE STUDS @ 14" O.C. OFFSET AT CENTER POINT.
 5. PHASES 1&2 INCLUDE MOBILE SPS INSTALLATION AND REMOVAL. SEE DRAWINGS GI-004 FOR COMPLETE PHASING PLAN.

Revisions:	Date:

CONSULTANT

ENGINEER OF RECORD
FELENER
ENGINEERING LLP
PROJECT # 19-263
22 Mulberry St, Suite 2A,
Madison, NJ 07940
1.845.343.1481 N.J. REG. 343-4966
UNAUTHORIZED ALTERATION OR ADDITION TO A PLAN
BEARING A LICENSED PROFESSIONAL ENGINEER'S SEAL
IS A VIOLATION OF STATE EDUCATION LAW.

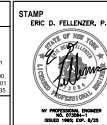


Office of
Construction
and Facilities
Management
VA U.S. Department
of Veterans Affairs

Drawing Title
ARCHITECTURAL:
INTERIOR ELEVATIONS
Approved: Project Director

Phase
100% FOR
CONSTRUCTION

Project Title VA SYRACUSE REPAIR SPS DEFICIENCIES	Project Number 528A7-19-720
Location VAMC, SYRACUSE, NY	Drawing Number 1
Issue Date 02-21-2025	Checked EDF
Drawn SRB	AS-504 PAGE: 22 OF 99

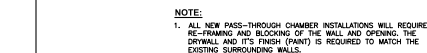

Technical drawing of a drywall grid system. The drawing shows a perspective view of the grid structure. Key components labeled include:

- GASKETED TYPE ACCESS PANEL
- EXPOSED TEE GRID SYSTEM - CROSS TEE
- FIELD ROUTE TO ACCOMMODATE ACCESS DOOR DIMENSIONS
- DRYWALL GRID SYSTEM MAIN BEAM
- DRYWALL GRID SYSTEM CROSS TEE

A cross-sectional diagram of a floor assembly. At the top, a thin, light-colored layer is labeled "RESINOUS FLOORING". Below this is a thick, textured layer labeled "Concrete". A diagonal line separates the concrete from a lower layer labeled "CHASE, OR SUBMITTAL CONCRETE". The chase layer is also textured and contains small, dark, irregular shapes. The entire assembly is shown within a rectangular frame.

RESINOUS FLOORING

WELDED SEAM SHEET FLOORING

CHISEL OR SAWCUT CONCRETE

DEPTH OF CUT INTO CONCRETE NECESSARY TO MATCH THE TWO FLOORING MATERIALS. HEIGHTS A SMOOTH AND FLUSH TRANSITION MUST BE ACHIEVED

Revisions:
Date:



NOTE: CEILING GRID HANGING WIRE
4"-0" ON CENTER EACH WAY (MAX.)

HANGER WIRE 12 GAUGE GALVANIZED STEEL WIRE -
WRAP THREE FULL TIMES LEAVING NO PISTALS ON WIRE

WALL ANGLE

CROSS "T"

MAIN RUNNER

ACOUSTICAL LAY-IN
CEILING PANEL


ACOUSTICAL TILE CEILING, HEIGHT PER PLANS
2' x 4' TEGULAR (DROPPED EDGE) ACOUSTICAL CEILING TILES

Diagram illustrating Shortspan Drywall Framing. The diagram shows a Tee fitting (labeled "SHORTSPAN TEE") connecting a vertical stud to a horizontal runner. A curved line indicates the placement of "1" GYPSUM BOARD" over the framing.

The image contains three technical drawings illustrating wall construction details:

- Top Drawing:** A cross-section of a wall assembly. It shows a metal stud (7/8" wide) with a 3/4" gap between studs. The wall is composed of ceramic tile, cement backer board, and caulk. A standard frame is shown on the right. Labels include: METAL STUD, PER SIG DTL OR 11/16"-D1, CERAMIC TILE, CEMENT BACKER BOARD, CAULK, STANDARD FRAME, TILE FINISH, ANCHOR, and JAMB ANCHORS.
- Bottom Left Drawing:** A cross-section of a wall assembly. It shows a metal stud (7/8" wide) with a 1/4" gap between studs. The wall is composed of double gypsum (GYP) and paint on gypsum base. A standard frame is shown on the right. Labels include: METAL STUD, DOUBLE GYP, 1/4", PAINT ON GYPSUM BASE, STANDARD FRAME, ANCHOR, and METAL STUD AND FINISH GYPSUM.
- Bottom Right Drawing:** A cross-section of a wall assembly. It shows a metal stud (7/8" wide) with a 1/4" gap between studs. The wall is composed of double gypsum (GYP) and paint on gypsum base. A standard frame is shown on the right. Labels include: METAL STUD, DOUBLE GYP, 1/4", PAINT ON GYPSUM BASE, STANDARD FRAME, ANCHOR, and METAL STUD AND FINISH GYPSUM.

ENGINEER OF RECORD	
	
FE PROJECT #: 19-263 22 Machinery St., Suite 2A Middletown, NY 10940 1 845-343-1681 fx 845-343-4995	www.fellp.com 181 Church St., Suite 100 Poughkeepsie, NY 12601 1 845-454-8704 fx 855-320-8735
UNAUTHORIZED ALTERATION OR ADDITION TO A PLAN BEARING A LICENSED PROFESSIONAL ENGINEER'S SEALS	

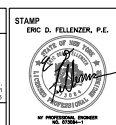

Office of
Construction
and Facilities
Management

U.S. Department
of Veterans Affairs

Drawing Title
ARCHITECTURAL DETAILS
Approved: Project Director

Approved: Project Director

Phase	100% FOR CONSTRUCTION
-------	-----------------------

Project Title	VA SYRACUSE REPAIR SPS DEFICIENCIES
---------------	--

Location	VAMC, SYRACUSE, NY
----------	--------------------

Issue Date
02-21

Checked
EDF

Project Number	528A7-19-720
----------------	--------------

Building Number

Drawing Number	
----------------	--

AS-701