


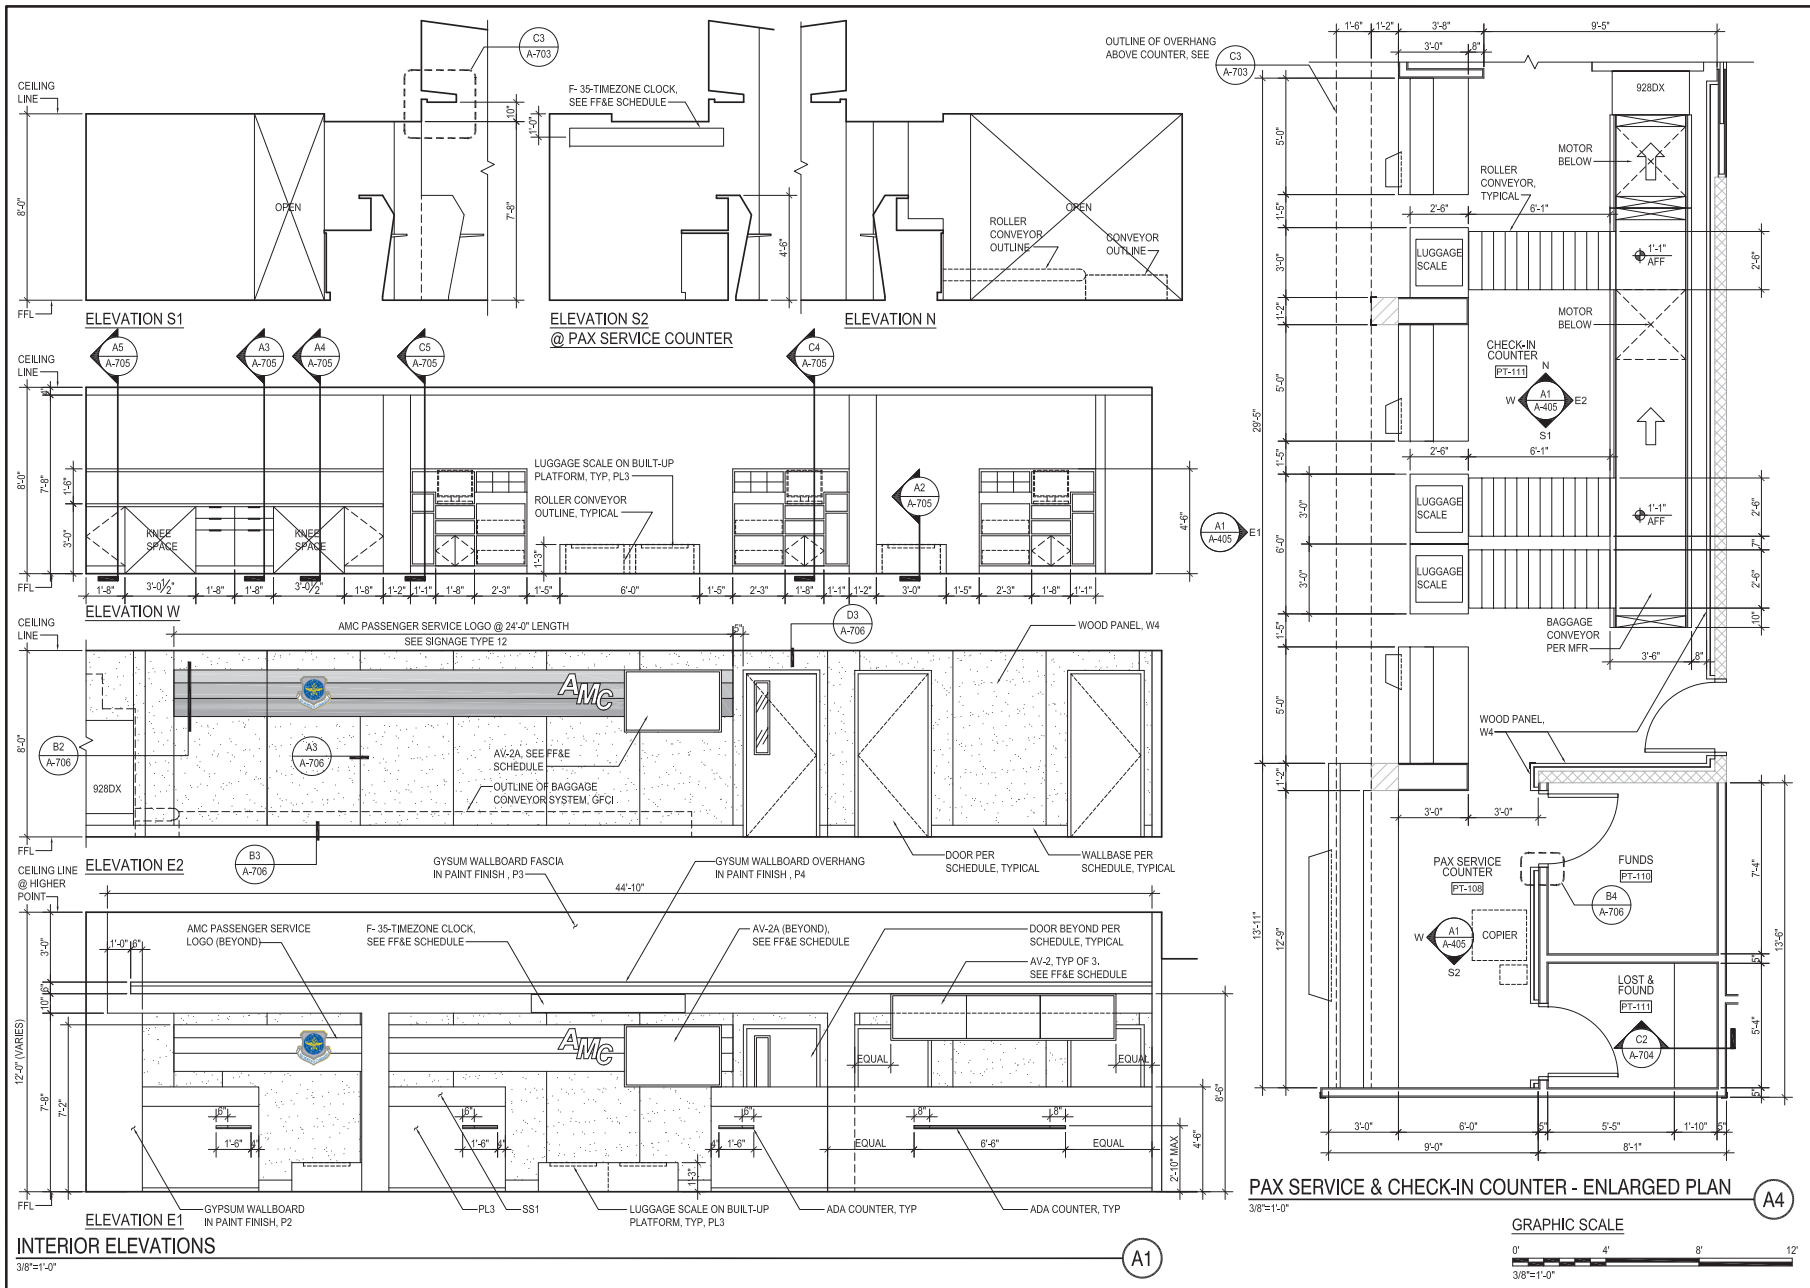

ANDERSEN AIR FORCE BASE

PROJECT TITLE:
RENOVATE PAX TERMINAL
B17002

AAFB PROJECT NUMBER: GUM
AJJY 19-004

APPROVED: BASE CIVIL ENGINEER

RECOMMENDED

SUBMITTED

CHIEF OF ENGINEERING

CHIEF OF OPERATIONS

CORROSION ENGINEER

CHIEF, CONSTRUCTION

ENVIRONMENTAL

BIOENVIRONMENTAL ENGINEER

GROUND SAFETY


FIRE CHIEF

COMMUNICATIONS

USING AGENCY

PROGRAM MANAGER

DOC MANAGER

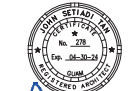

Signature

ARCHITECTS - ENGINEERS

I CERTIFY THAT THIS WORK
WAS PREPARED BY ME OR
UNDER MY DIRECT SUPERVISION

SHEET TITLE
PAX SERVICE &
CHECK-IN COUNTER -
ENLARGED PLAN &
INTERIOR ELEVATIONS

DESIGNED: MKG/MBB DATE: 5/12/2023

SHEET: JST SCALE: AS SHOWN

SHEET A-405 SHEET 40 OF 153

REVISIONS BY DATE

REVISIONS	BY	DATE

DWG ACAD NUMBER

FILE NO.

FINAL DESIGN SUBMITTAL