



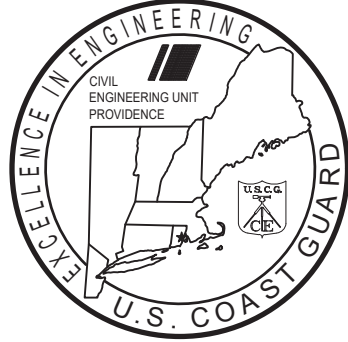


U.S. COAST GUARD
CIVIL ENGINEERING
CEU PROVIDENCE



BASE CAPE COD - HQ & AIRFIELD
BUZZARDS BAY, MASSACHUSETTS
16677450 REPLACE MEDIUM VOLTAGE
TRANSFORMER CUTOFF SWITCHES
ELECT DIST SYSTEM (ALL)

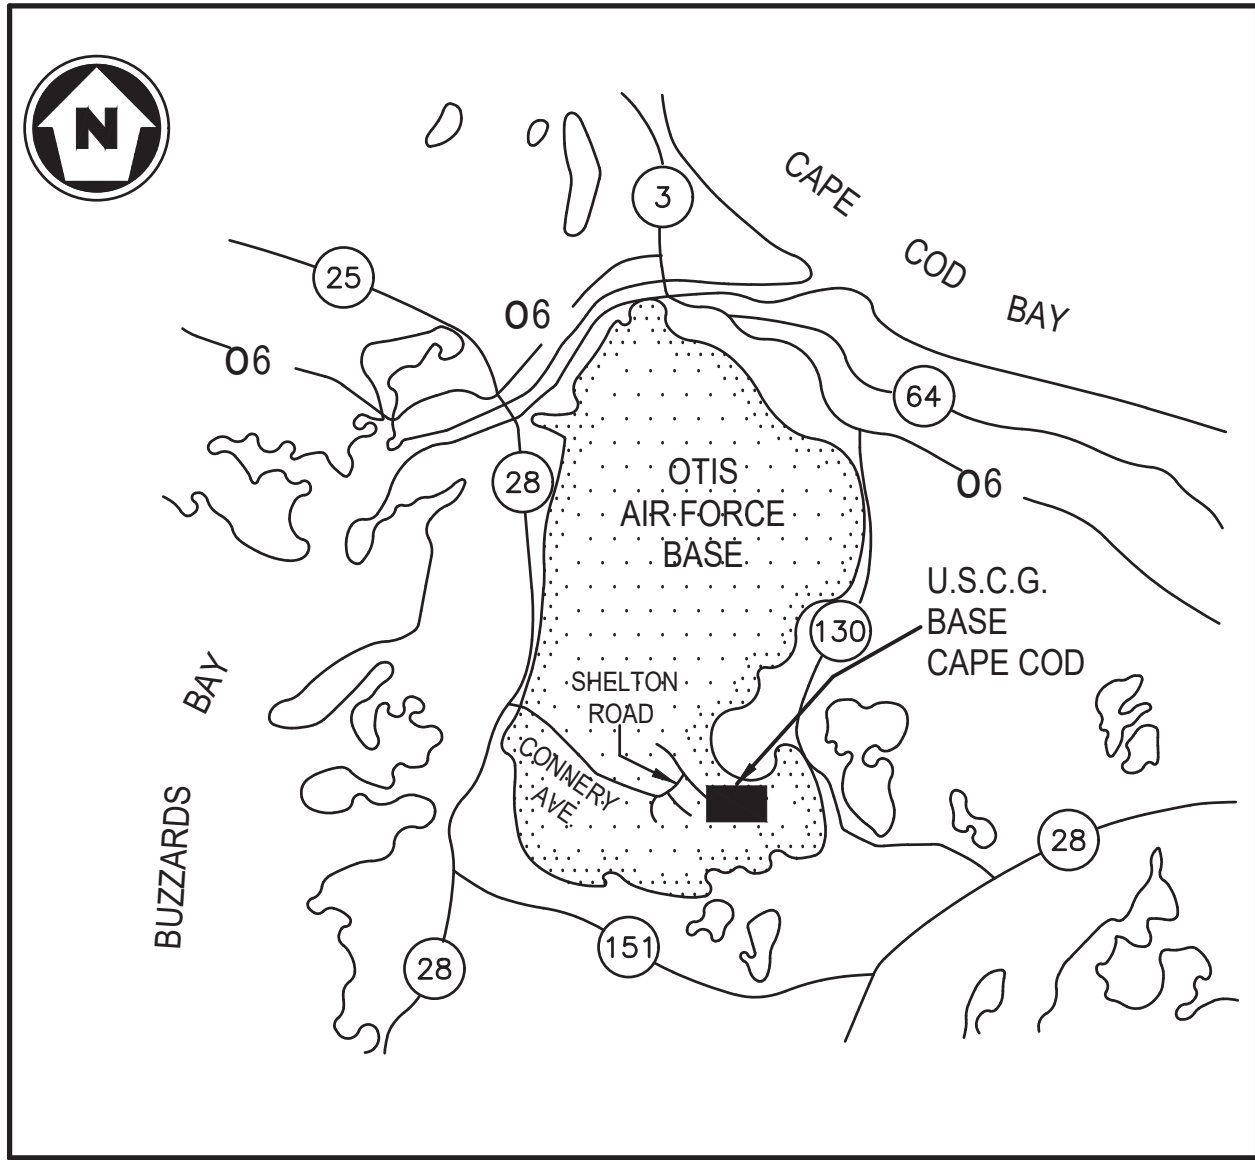

VICINITY MAP
SCALE: NTS

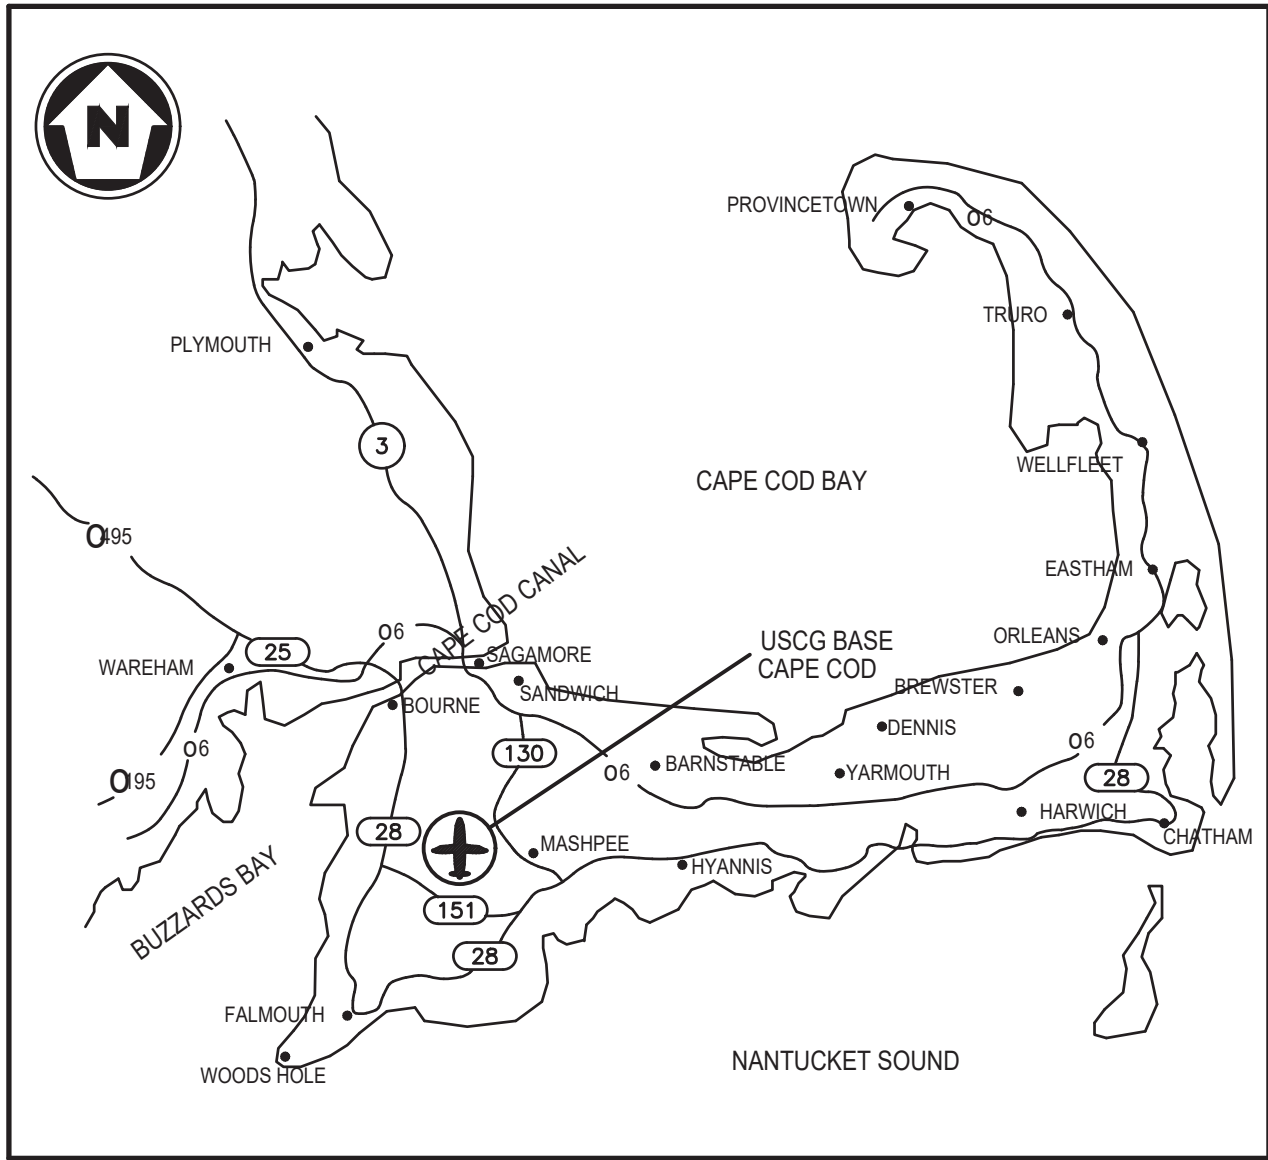

LOCATION MAP
SCALE: NTS

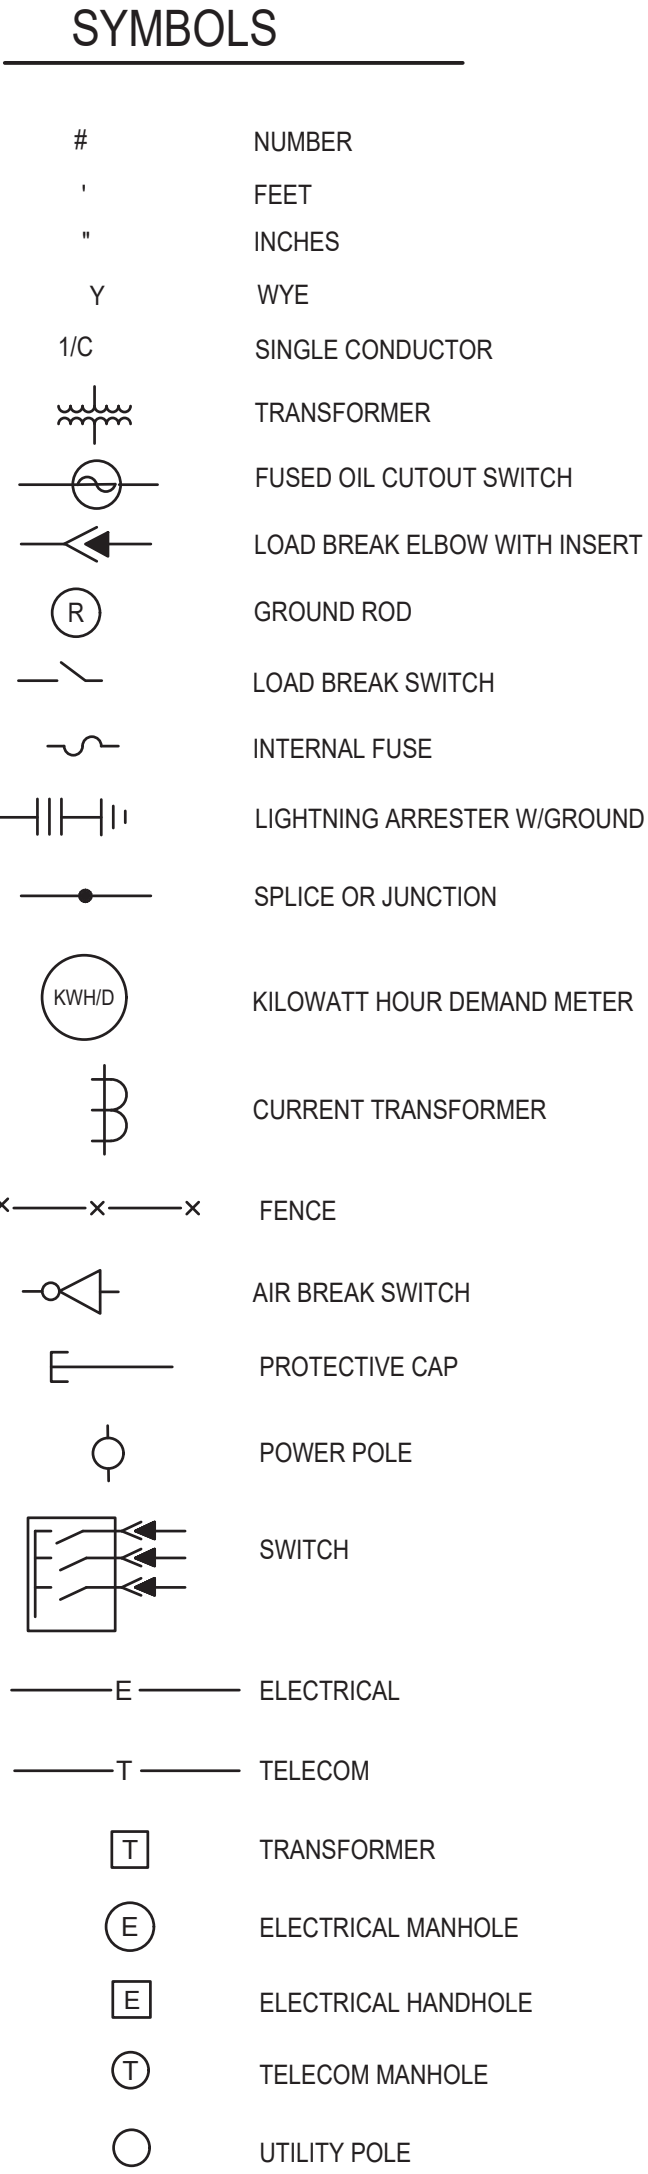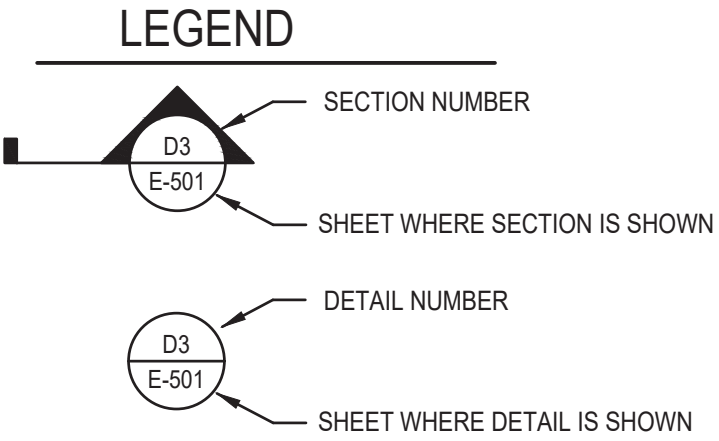

ABBREVIATIONS

BLDG	BUILDING
E.M.H.	ELECTRICAL MANHOLE
H.H.	HANDHOLE
N.T.S.	NOT TO SCALE

MICHAEL P. CAROSOTTO, PE
APPROVING OFFICIAL
DATE

MICHAEL P. CAROSOTTO, PE
TECHNICAL DIRECTOR

DAVID DILL, PE
BRANCH CHIEF

DRAWING INDEX		
SHEET ID	SHEET #	SHEET TITLE
G-001	01	COVER SHEET
E-101	02	SITE PLAN
E-401	03	ENLARGED SITE PLANS
E-501	04	DETAILS
E-601	05	ONE LINE DIAGRAM





ISSUED FOR BIDDING	JAN 2026	DATE
0	MARK	DESCRIPTION
MEASUREMENT BAR: 1" = 1' (HALF SIZE = 1/2")		

A/E COMPANY:	A/E PROJECT NO.:	CONSULTING A/E:
USCG CEU PROVIDENCE 475 KILVERT ST., SUITE 100 WARWICK, RI 02886	16677450	TESSIER, JOSHUA
USCG PROJECT NUMBER 16677450	USCG DRAWING SERIES NUMBER P16677450	USCG FILENAME P16677450-C01.dwg
DESIGNED BY: JIM	DRAWN BY: JIM	CHECKED BY: JIM
EDITED BY: JIM	DATE: 05	SHEET: 01 OF 05

REPLACE MEDIUM VOLTAGE TRANSFORMER CUTOFF SWITCHES BASE CAPE COD - HQ & AIRFIELD BUZZARDS BAY	MA GENERAL COVER SHEET
---	------------------------------

SHEET ID ELECT DIST SYSTEM (ALL) G-001

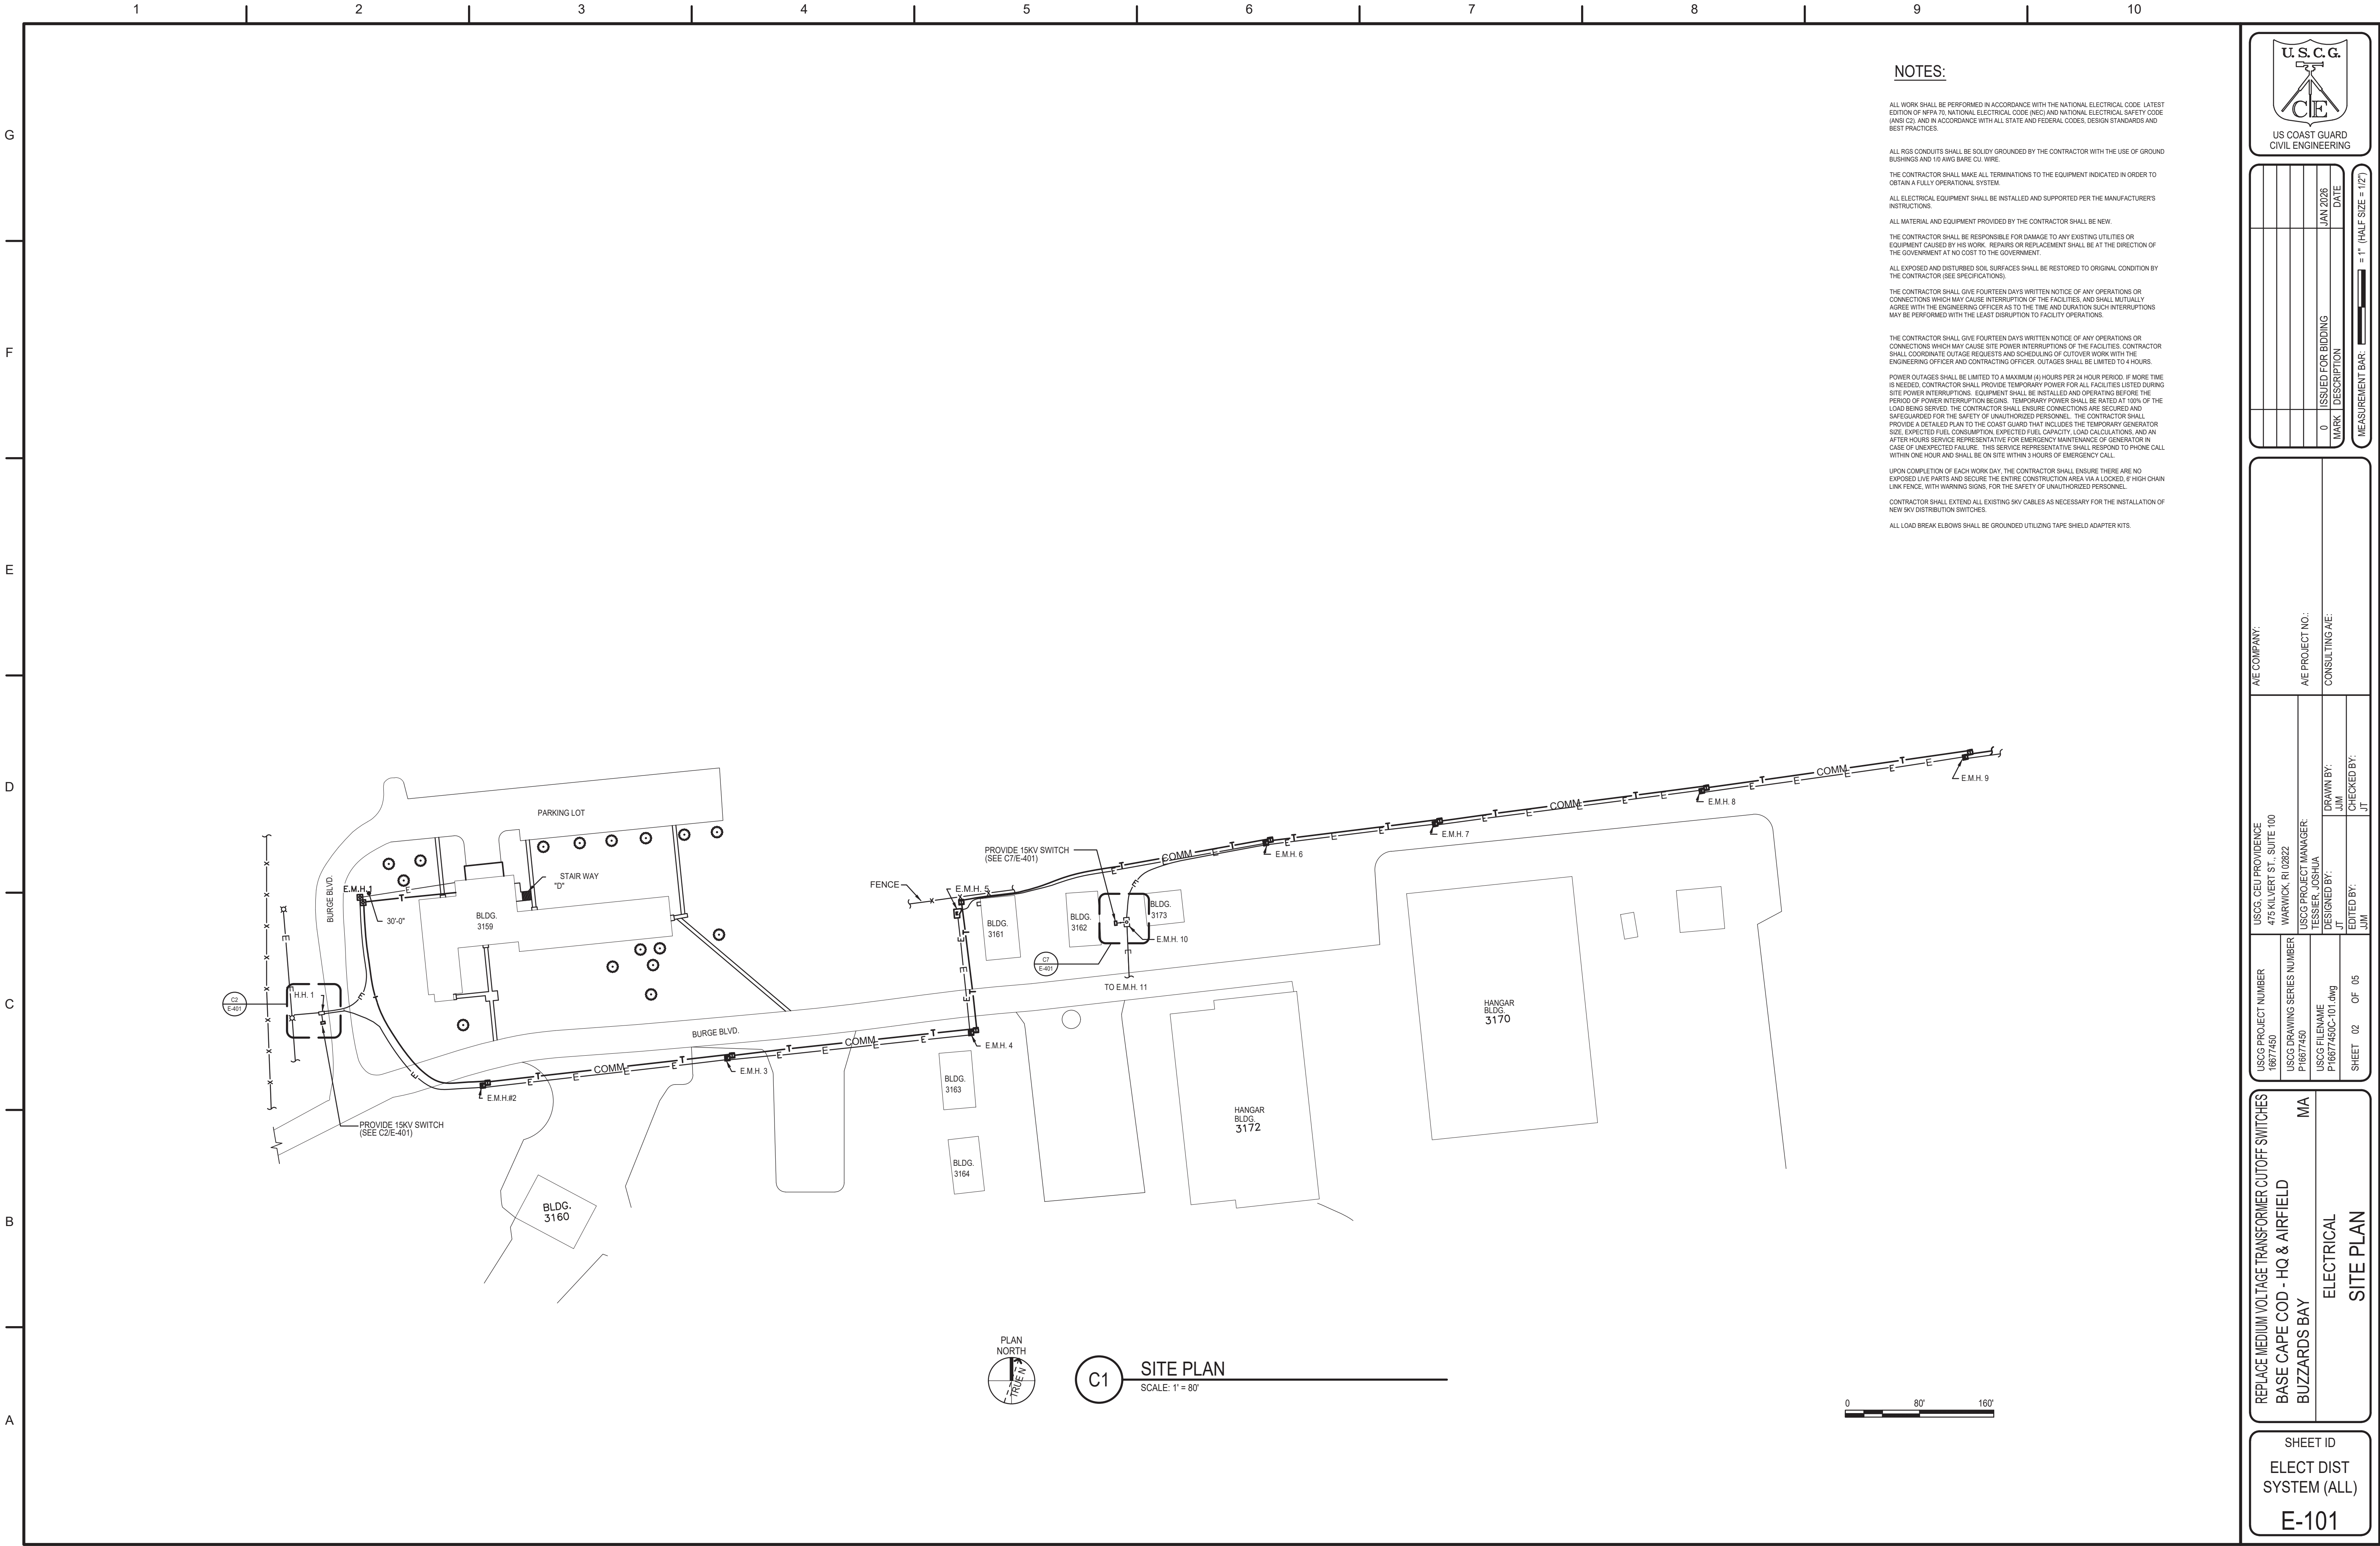

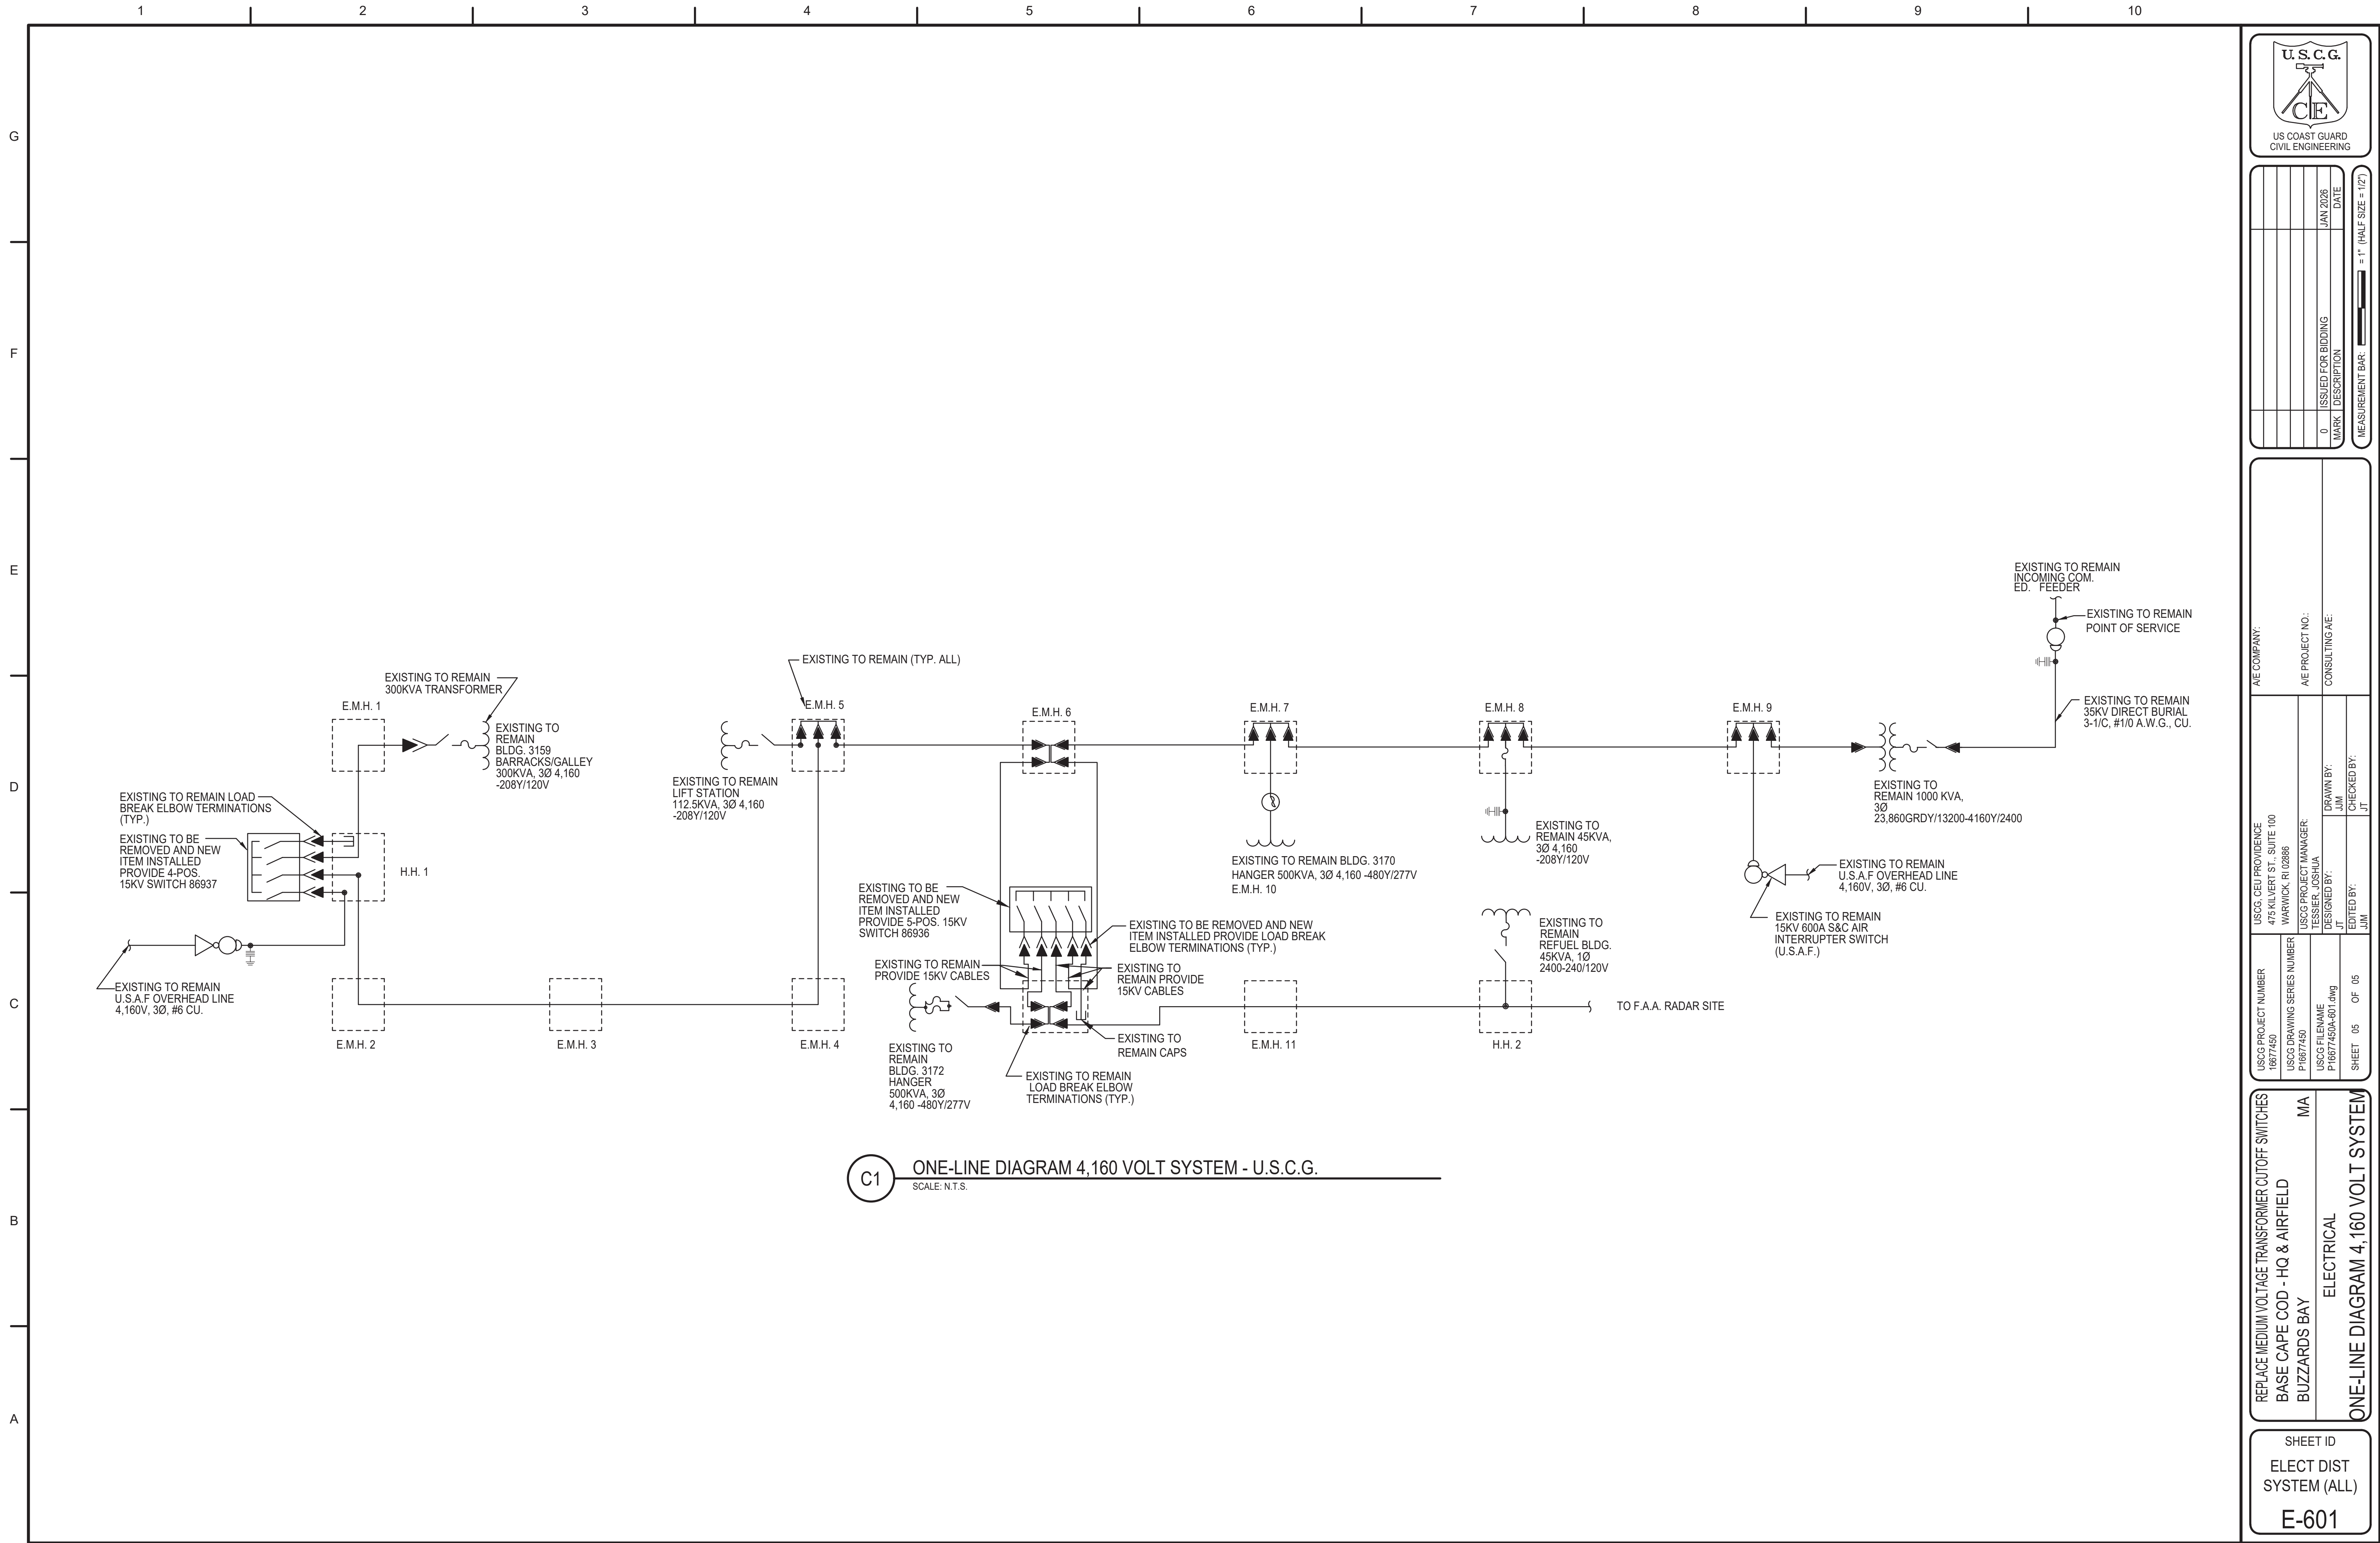



U.S.C.G.
US COAST GUARD
CIVIL ENGINEERING

MARK	DESCRIPTION	JAN 2026	DATE
0	ISSUED FOR BIDDING		

MEASUREMENT BAR: 1" = 1' (HALF SIZE = 1/2")

A/E COMPANY:		A/E PROJECT NO.:		CONSULTING A/E:	
USCG CEU PROVIDENCE		475 KILVERT ST., SUITE 100		WARWICK, RI 02886	
USCG PROJECT NUMBER		16677450		USCG DRAWING SERIES NUMBER	
P16677450		P16677450		P16677450	
USCG FILENAME		P16677450-401.dwg		DESIGNED BY:	
J.M.		J.T.		CHECKED BY:	
J.M.		J.T.		J.M.	
SHEET 05		OF 05			

REPLACE MEDIUM VOLTAGE TRANSFORMER CUTOFF SWITCHES
BASE CAPE COD - HQ & AIRFIELD
BUZZARDS BAY

MA

ELECTRICAL

ONE-LINE DIAGRAM 4,160 VOLT SYSTEM

SHEET ID
ELECT DIST
SYSTEM (ALL)
E-601