


FILE NAME: P:\Federal\NAVFAC\Mainland\Utilities\DD\TO 0007 - 872 Description Print\05 Design Services\BNA-CAD\Site-CAD\NAVFAC-V-104-Bldg 242-72 Survey Plans.dwg PLOTTED: Friday, August 15, 2025 - 5:56pm USER: Connor.Matthew

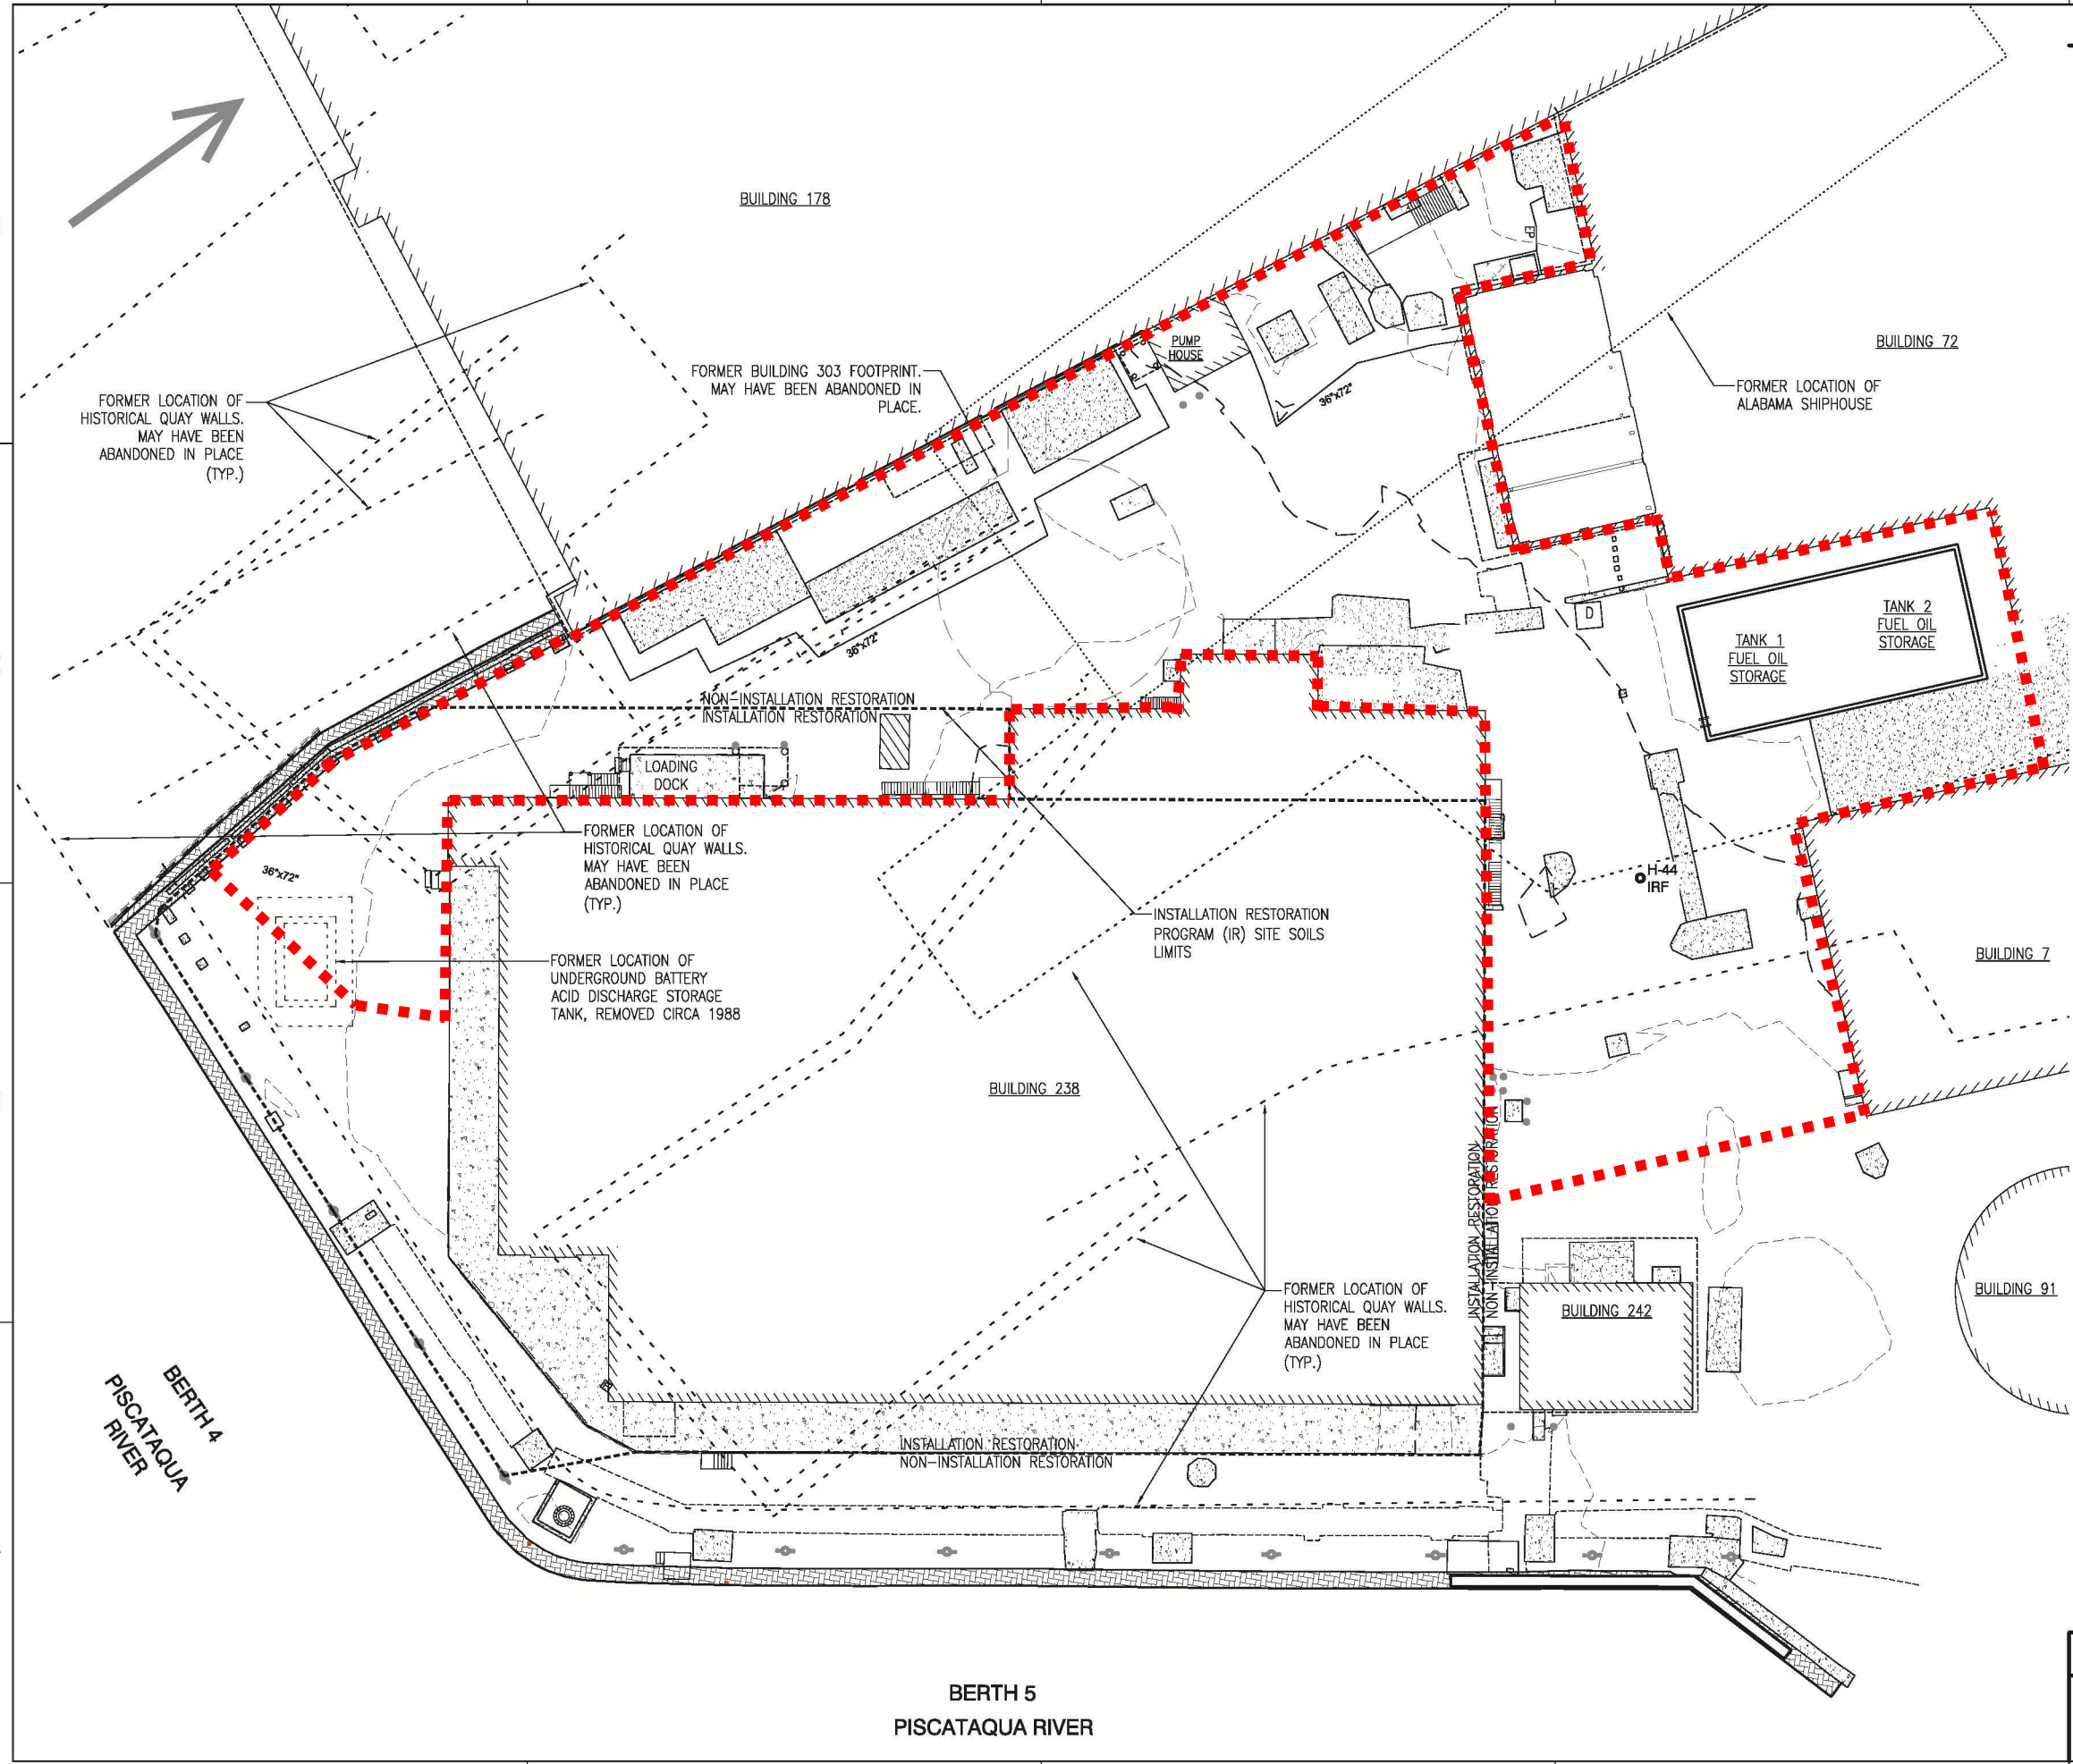

GENERAL SHEET NOTES

1. WORK DEPICTED HEREIN MAY BE LOCATED WITHIN AN ENVIRONMENTAL, NATURAL HISTORIC OR ARCHAEOLOGICAL RESOURCE AREA. REFER TO SHEET V-104 FOR INFORMATION ON THE BOUNDS OF THESE AREAS.
2. EXCAVATED MATERIALS MUST BE MANAGED ACCORDING TO THE PORTSMOUTH NAVAL SHIPYARD'S CURRENT SOIL MANAGEMENT STANDARD OPERATING PROCEDURE (LATEST EDITION).
3. EXCAVATED MATERIAL FROM IR AREAS WILL REQUIRE SEPARATE MANAGING AND DISPOSAL FROM EXCESS MATERIALS GENERATED OUTSIDE IR SITE BOUNDARIES. REUSE OF EXCAVATION SOIL IN IR AREAS IS PROHIBITED.



APPROVED	
FOR COMMANDER NAVFAC	
ACTIVITY	
SATISFACTORY TO DATE	
DESIGNER	MTG
DRAWN BY	RS
CHECKED BY	MEC
DESIGN MANAGER	JTL
PROJECT MANAGER	LST
DESIGN DIRECTOR	MHR
FIRE PROTECTION	SSR

NAVAL FACILITIES ENGINEERING SYSTEMS COMMAND
NAVFAC
PUBLIC WORKS DEPARTMENT - MAINE
PORTSMOUTH NAVAL SHIPYARD
KITTERY, MAINE
CONTRACT NUMBER: TBD
P-1112 B72 RESILIENCY IMPROVEMENTS
HISTORICAL QUAY WALLS AND BUILDING FOUNDATION PLANS

PROJECT NO.:	1710371
NAVFAC DRAWING NO.:	#####
SHEET	19 OF 226
V-104	FAC-YR-NUM

DRAWING REVISION: 07 AUG 2016