



2150 NOLIN DAM ROAD
MAMMOTH CAVE, KY 42259
NOLIN RIVER LAKE HOIST REPLACEMENT

P2 515776

SHEET INDEX	
SHEET NUMBER	SHEET NAME
G-001	COVER SHEET
G-002	VICINITY MAPS
G-003	PROPOSED SITE ACCESS, HAUL ROUTE AND LAYDOWN AREA
S-001	GENERAL STRUCTURAL NOTES, DESIGN LOADS & ABBREVIATIONS
SD-111	DEMOLITION PLAN AND DETAILS
S-111	FRAMING PLAN
S-301	CRANE REFERENCE DIAGRAM
S-531	FRAMING SECTIONS AND DETAILS
P-001	PLUMBING LEGEND
PD-111	PIPING DEMOLITION
P-111	PIPING NEW WORK
E-001	GENERAL ELECTRICAL NOTES AND LEGEND
E-101	ELECTRICAL PLANS
E-601	ELECTRICAL DETAILS



SOLICITATION NO.: TBD

CONTRACT NO.: TBD

ISSUE DATE: 02-24-2025

VOLUME: 1 OF 1

01 May 2025
W912QR25BA014

[illegible]

LOUISVILLE DISTRICT 600 DR MARTIN LUTHER KING JR. PLACE LOUISVILLE, KY 40202	Z. HORN BY: Z. HORN		SOLICITATION NO.: 02-24-2025
	CHECKED BY: M. WILSON		CONTRACT NO.: TBD
SUBMITTED BY: J. ESTERLE		SIZE: ANSI D	

WARREN COUNTY, N.Y. 14220
NOLIN RIVER LAKE HOIST REPLACEMENT
P2 515776
COVER SHEET

SHEET ID

G-001

SIGNATURES AFFIXED BELOW INDICATE
OFFICIAL RECOMMENDATION AND
APPROVAL OF ALL DRAWINGS IN THIS SET.

APPROVAL RECOMMENDED: *

ZACHARY HORN, PE

TECHNICAL LEAD

Digitally signed by HORN,ZACHARY TYLER, 1628203102
DN: cn=ZACHARY TYLER, 1628203102, o=USA,
ou=U.S. GOVERNMENT, ou=U.S. GOVERNMENT, cn=ZACHARY TYLER, 1628203102

HORN,ZACHARY TYLER, 1628203102





*APPROVAL RECOMMENDED SIGNATURE
INDICATES DESIGN AND QUALITY CONTROL
REVIEWS ARE COMPLETE, INCLUDING
ITR/ATR CERTIFICATION.

APPROVED: **

IAN F. MITCHELL, PE

CHIEF, ENGINEERING DIVISION

** THIS PROJECT WAS DESIGNED BY THE U.S.
ARMY CORPS OF ENGINEERS, LOUISVILLE
DISTRICT.
INDIVIDUALS WHOSE SIGNATURES AND
REGISTRATION DESIGNATIONS APPEAR ON
THESE DOCUMENTS ARE OPERATING WITHIN
THE SCOPE OF THEIR EMPLOYMENT.
SIGNATURES ARE REQUIRED BY
ER 1110-1-8152.

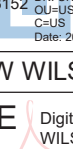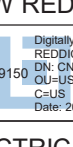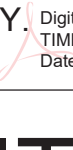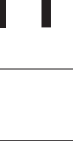SIGNATURES AFFIXED BELOW INDICATE OFFICIAL RECOMMENDATION AND APPROVAL OF ALL DRAWINGS IN THIS SET.	
STRUCTURAL	
DESIGNER: ZACHARY HORN, PE	
	Digitally signed by ZACHARY HORN, PE DN: cn=ZACHARY TYLER 1623933152, o=State of Georgia, ou=Professional Engineer, email=ZACHARY TYLER 1623933152@GA.GOV, c=US
CHECKER: MATTHEW WILSON, PE	
	Digitally signed by WILSON MATTHEW G. 1634055483 Date: 2025.03.19 08:39:36 -0400
PLUMBING/MECHANICAL	
DESIGNER: BRETT HARTMAN	
	Digitally signed by HARTMAN BRETT E. 1548512618 cn=BRETT HARTMAN BRETT E. 1548512618, o=GA, ou=State of Georgia, ou=Professional Engineer, email=
CHECKER: MATTHEW REDDICK, PE	
	Digitally signed by REDDICK MATTHEW REDDICK 1242491516 cn=MATTHEW REDDICK 1242491516, o=State of Georgia, ou=Professional Engineer, email=
ELECTRICAL	
DESIGNER: LONDON ALEXANDER, PE	
	Digitally signed by ALEXANDER LONDON A. 1538722460 Date: 2025.03.18 16:57:51 -0400
CHECKER: JEFFREY TIMBAS, PE	
	Digitally signed by TIMBAS JEFFREY W. 1365057903 Date: 2025.03.19 08:38:49 -0400

CERTIFIED FINAL SUBMITTAL



A
B
C
D
E
F
G
H
J
K
L
M
N
P



A
B
C
D
E
F
G
H
J
K
L
M
N
P

1. CONTACT THE CONTRACTING OFFICER TO REQUEST CHANGING THE PROPOSED SITE ACCESS AND HAUL ROUTE.
2. CONTACT THE CONTRACTING OFFICER TO REQUEST CHANGING THE LOCATION OF OR EXPANDING THE SIZE OF THE PROPOSED LAYDOWN AREA.
3. THE SAFE LOAD CAPACITY OF THE SERVICE BRIDGE IS 40,000 LBS TOTAL. ALL LOADS EXCEEDING 30,000 LBS MUST BE SUBMITTED TO AND APPROVED BY THE CONTRACTING OFFICER PRIOR TO BEING APPLIED TO THE SERVICE BRIDGE.
4. NO VEHICLES, MATERIALS OR EQUIPMENT MAY BE STORED ALONG ANY POINT OF THE SERVICE BRIDGE.
5. SEE SHEET S-001 FOR GENERAL NOTES.

[illegible]

US ARMY CORPS OF ENGINEERS LOUISVILLE DISTRICT 600 DR. MARTIN LUTHER KING JR. PLACE LOUISVILLE, KY 40202	DESIGNED BY: Z. HORN	ISSUE DATE: 02-24-2025
	CHECKED BY: Z. HORN	CITATION NO.: TBD
	CHECKED BY: M. WILSON	CONTRACT NO.: TBD
	SUBMITTED BY: J. ESTERLE	
	APPROVED: ANS/D	

2150 NOLIN DAM ROAD
MAMMOTH CAVE, KY 42259
NOLIN RIVER LAKE HOIST REPLACEMENT
P2 515776
PROPOSED SITE ACCESS, HAUL ROUTE AND
LAYDOWN AREA

SHEET ID

G-003

CERTIFIED FINAL SUBMITTAL W912QR25BA014 Plans-0000

Plot Date: 3/18/2025 2:53:52 PM
File Path: C:\Temp\515776_v2022_S_Zachary\Thom.rvt

US Army Corps of Engineers®

</



**US Army Corps
of Engineers®**

[illegible]

US ARMY CORPS OF ENGINEERS LOUISVILLE DISTRICT 600 DR. MARTIN LUTHER KING JR. PLACE LOUISVILLE, KY 40202	DESIGNED BY: Z. HORN	ISSUE DATE: 02-24-2025
	CHECKED BY: Z. HORN	SUB. CITATION NO.: TBD
	SUBMITTED BY: M. WILSON	CONTRACT NO.: TBD
	SIZE: ANSI D	

2150 NOLIN DAM ROAD
MAMMOTH CAVE, KY 42259
NOLIN RIVER LAKE HOIST REPLACEMENT
P2 516776

GENERAL STRUCTURAL NOTES, DESIGN LOADS &
ABBREVIATIONS

SHEET ID


S-001

C:\Temp\515776_v2022_S_Zachary.Lhom.rvt

File Path:

Plot Date: 3/18/2025 2:53:52 PM

CERTIFIED FINAL SUBMITTAL W912QR25BA014 Plans-0000

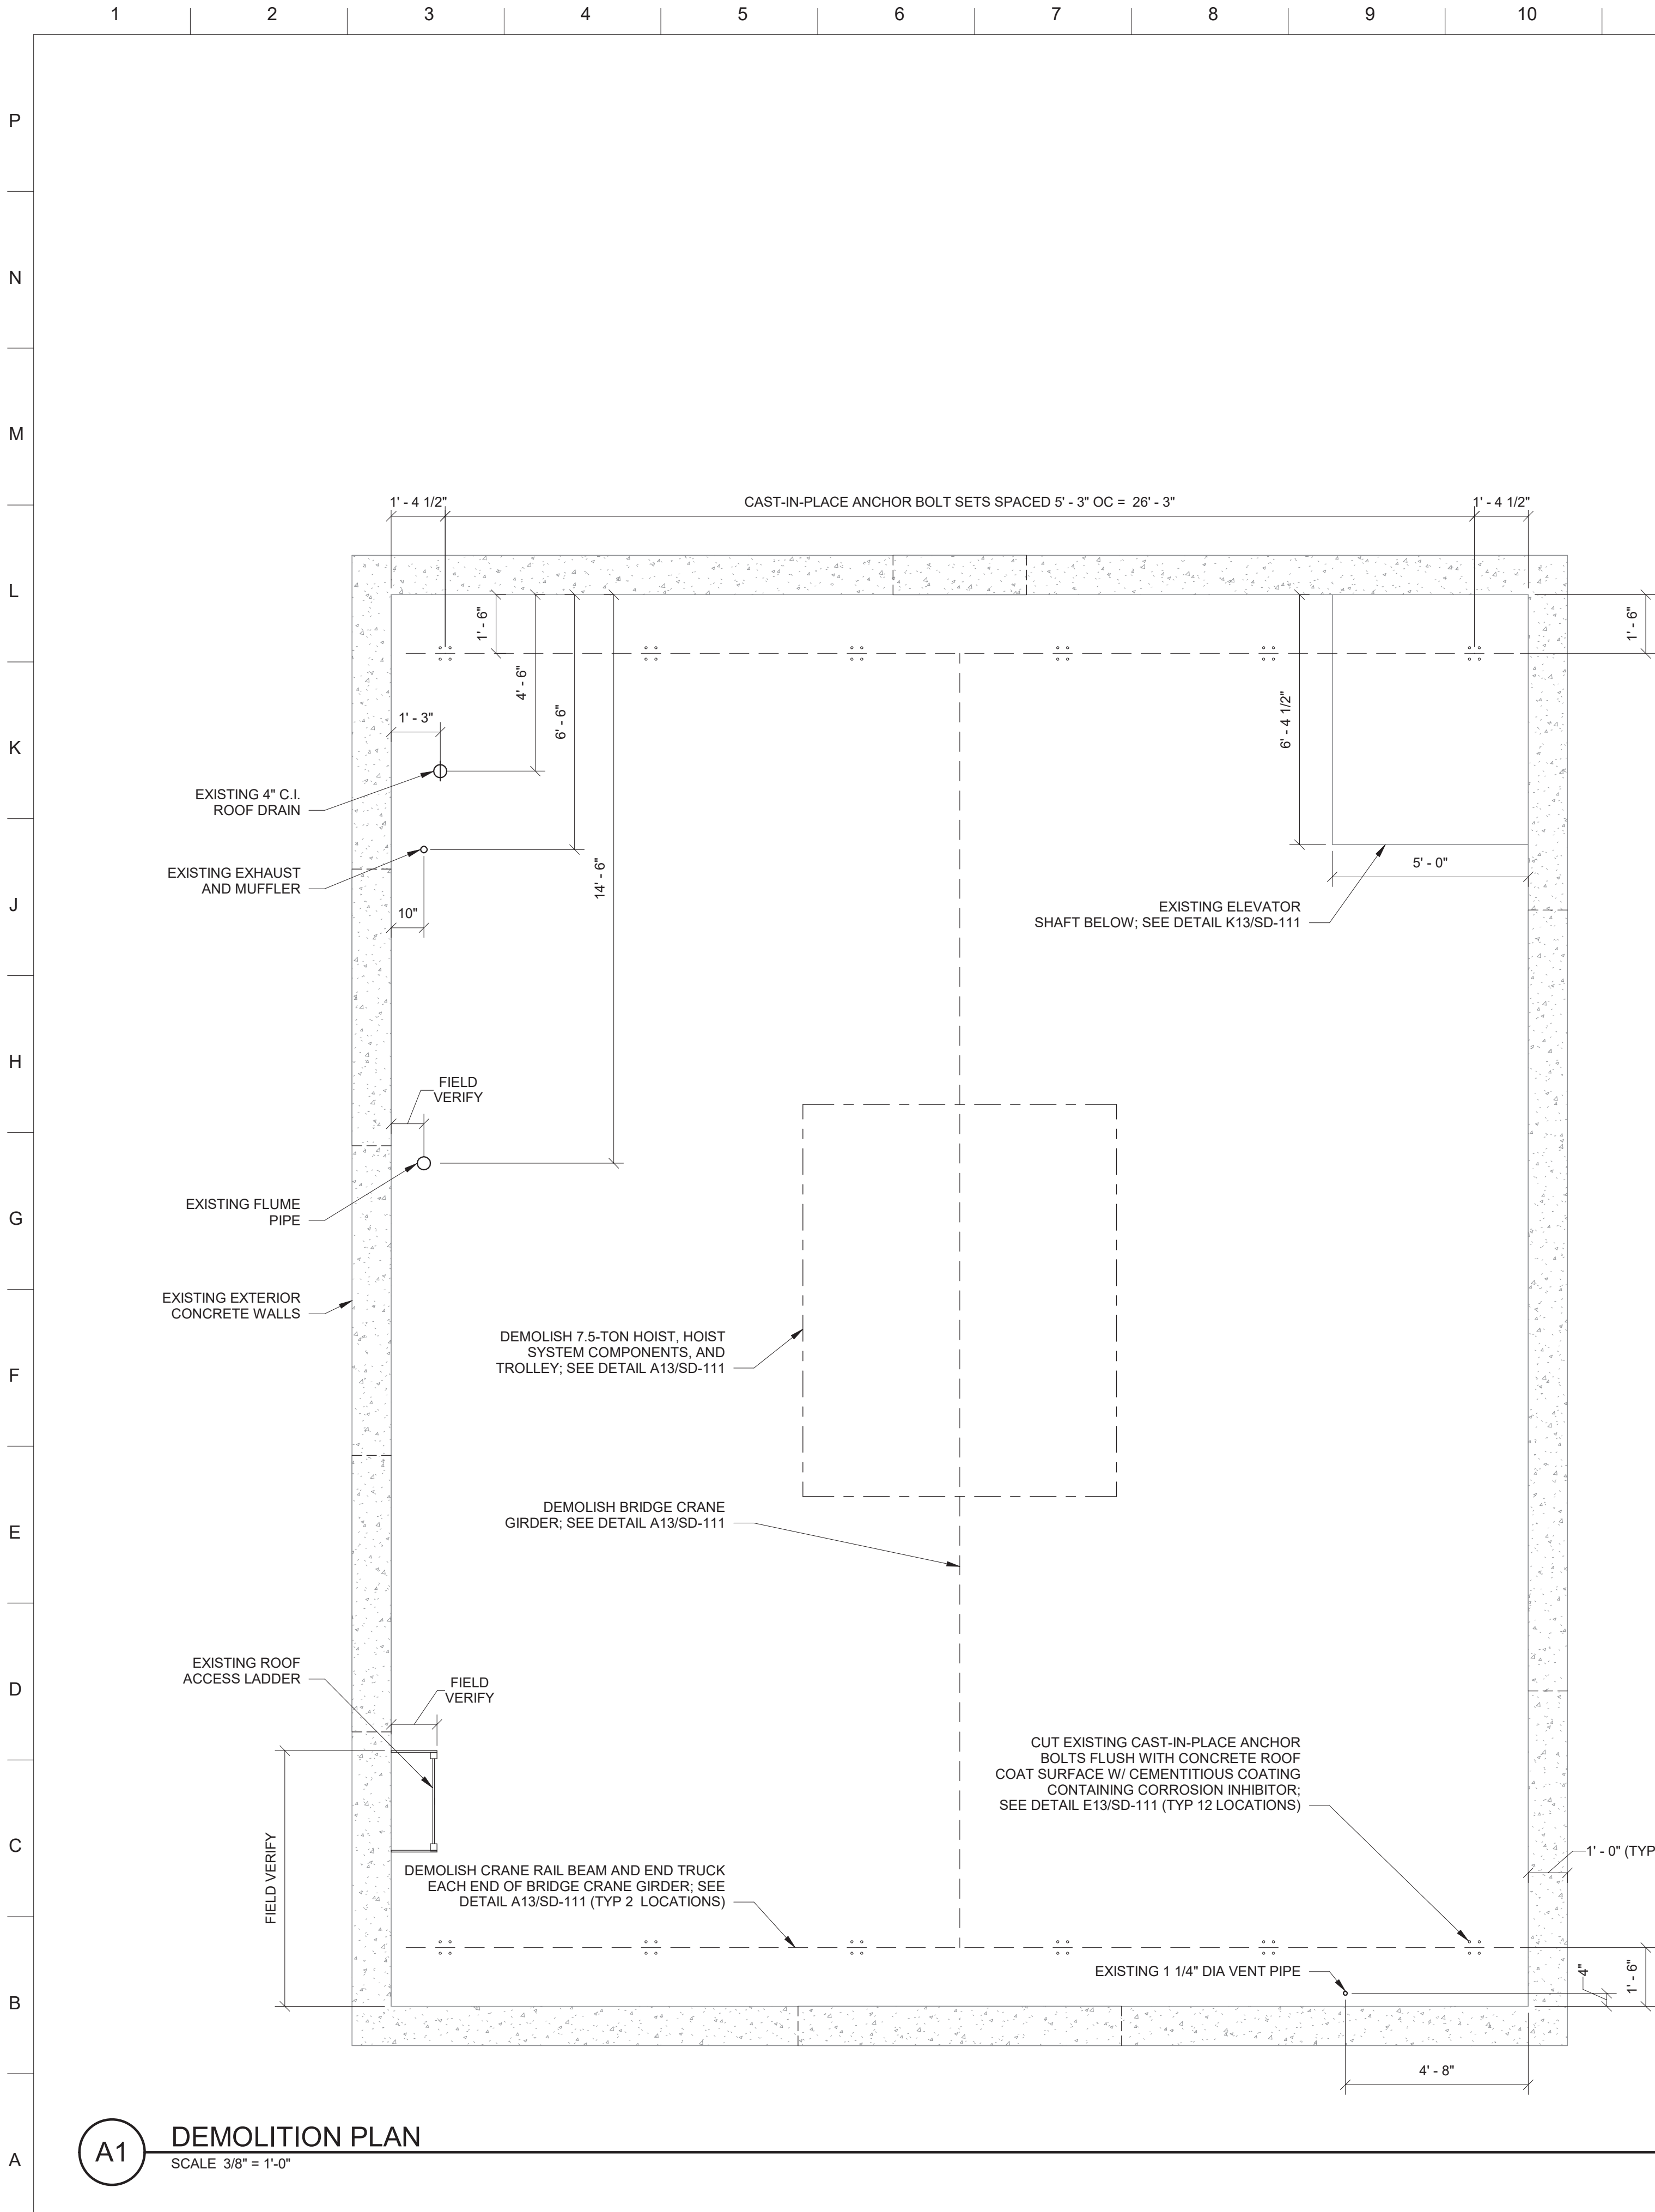

GENERAL SHEET NOTES

- ALL DIMENSIONS AND ELEVATIONS OF EXISTING ELEMENTS HAVE BEEN PROVIDED TO MATCH THE AS-BUILTS. WORK LIMITS FOR BOTH DEMOLITION AND NEW WORK ARE BETWEEN ELEVATIONS 581' AT THE OPERATING FLOOR TO 607.5' AT THE BOTTOM OF THE ROOF.
- REQUIREMENTS FOR DEMOLITION ARE PROVIDED IN SPECIFICATION 02 41 00 DEMOLITION AND THE SPECIFICATIONS REFERENCED THEREIN.
- THE CONTRACTOR MUST PREPARE A DEMOLITION PLAN IN ACCORDANCE WITH SPECIFICATION 02 41 00 DEMOLITION. THE CONTRACTOR'S DEMOLITION PLAN MUST BE APPROVED PRIOR TO ANY DEMOLITION WORK BEING PERFORMED.
- CONTACT THE CONTRACTING OFFICER PRIOR TO THE DEMOLISHING OR RELOCATING ANY EXISTING EQUIPMENT NOT IDENTIFIED FOR DEMOLITION OR RELOCATION IN THE CONSTRUCTION DRAWINGS.
- ELEVATOR SHAFT EQUIPMENT, LADDER, FLUME, AND EXHAUST PIPES ARE SHOWN FOR REFERENCE ONLY AND THE EXPECTATION IS THAT THIS EQUIPMENT WILL NOT CONFLICT WITH THE RAIL OR BRIDGE CRANE. REMAINING EXISTING EQUIPMENT ALONG WALLS AND ON OPERATING FLOOR NOT SHOWN FOR CLARITY. VERIFY MAX OBSTRUCTION DISTANCE IN FIELD. SEE AS-BUILTS FOR ADDITIONAL EXISTING EQUIPMENT INFORMATION.
- SEE SHEET S-001 FOR GENERAL NOTES.



EXISTING ELEVATOR SHAFT EQUIPMENT TO REMAIN

K13 EXISTING ELEVATOR DETAIL

SCALE: NTS



CUT EXISTING CAST-IN-PLACE ANCHOR BOLTS FLUSH WITH CONCRETE ROOF COAT SURFACE W/ CEMENTITIOUS COATING CONTAINING CORROSION INHIBITOR

EXISTING CRANE RAIL BEAM

E13 ANCHOR DEMOLITION DETAIL

SCALE: NTS



DEMOLISH CRANE RAIL BEAM AND END TRUCK EACH END OF BRIDGE CRANE GIRDER; SEE DETAIL E13/SD-111 FOR DEMOLITION OF CAST-IN-PLACE ANCHORS

DEMOLISH BRIDGE CRANE GIRDER

DEMOLISH 7.5-TON HOIST, HOIST SYSTEM COMPONENTS, AND TROLLEY

A13 CRANE DEMOLITION DETAILS

SCALE: NTS



US Army Corps
of Engineers ®

MARK	DESCRIPTION	DATE

DESIGNED BY: Z. HORN	ISSUE DATE: 02-24-2025
DRAWN BY: E. GARCIA	SOLICITATION NO.: TED
CHECKED BY: M. WILSON	CONTRACT NO.: TED
SUBMITTED BY: J. ESTERLE	SIZE: ANSI D
US ARMY CORPS OF ENGINEERS LOUISVILLE DISTRICT 600 DR. MARTIN LUTHER KING JR. PLACE LOUISVILLE, KY 40202	

2150 NOLIN DAM ROAD MAMMOTH CAVE, KY 42259 NOLIN RIVER LAKE HOIST REPLACEMENT P2 515776 DEMOLITION PLAN AND DETAILS

SHEET ID
SD-111


C:\temp\515776_0205_S_Zulway\1.htm.v4

File Path:

3/19/2025 2:53:55 PM


Plot Date:

CERTIFIED FINAL SUBMITTAL W912QR25BA014_Plans-0000

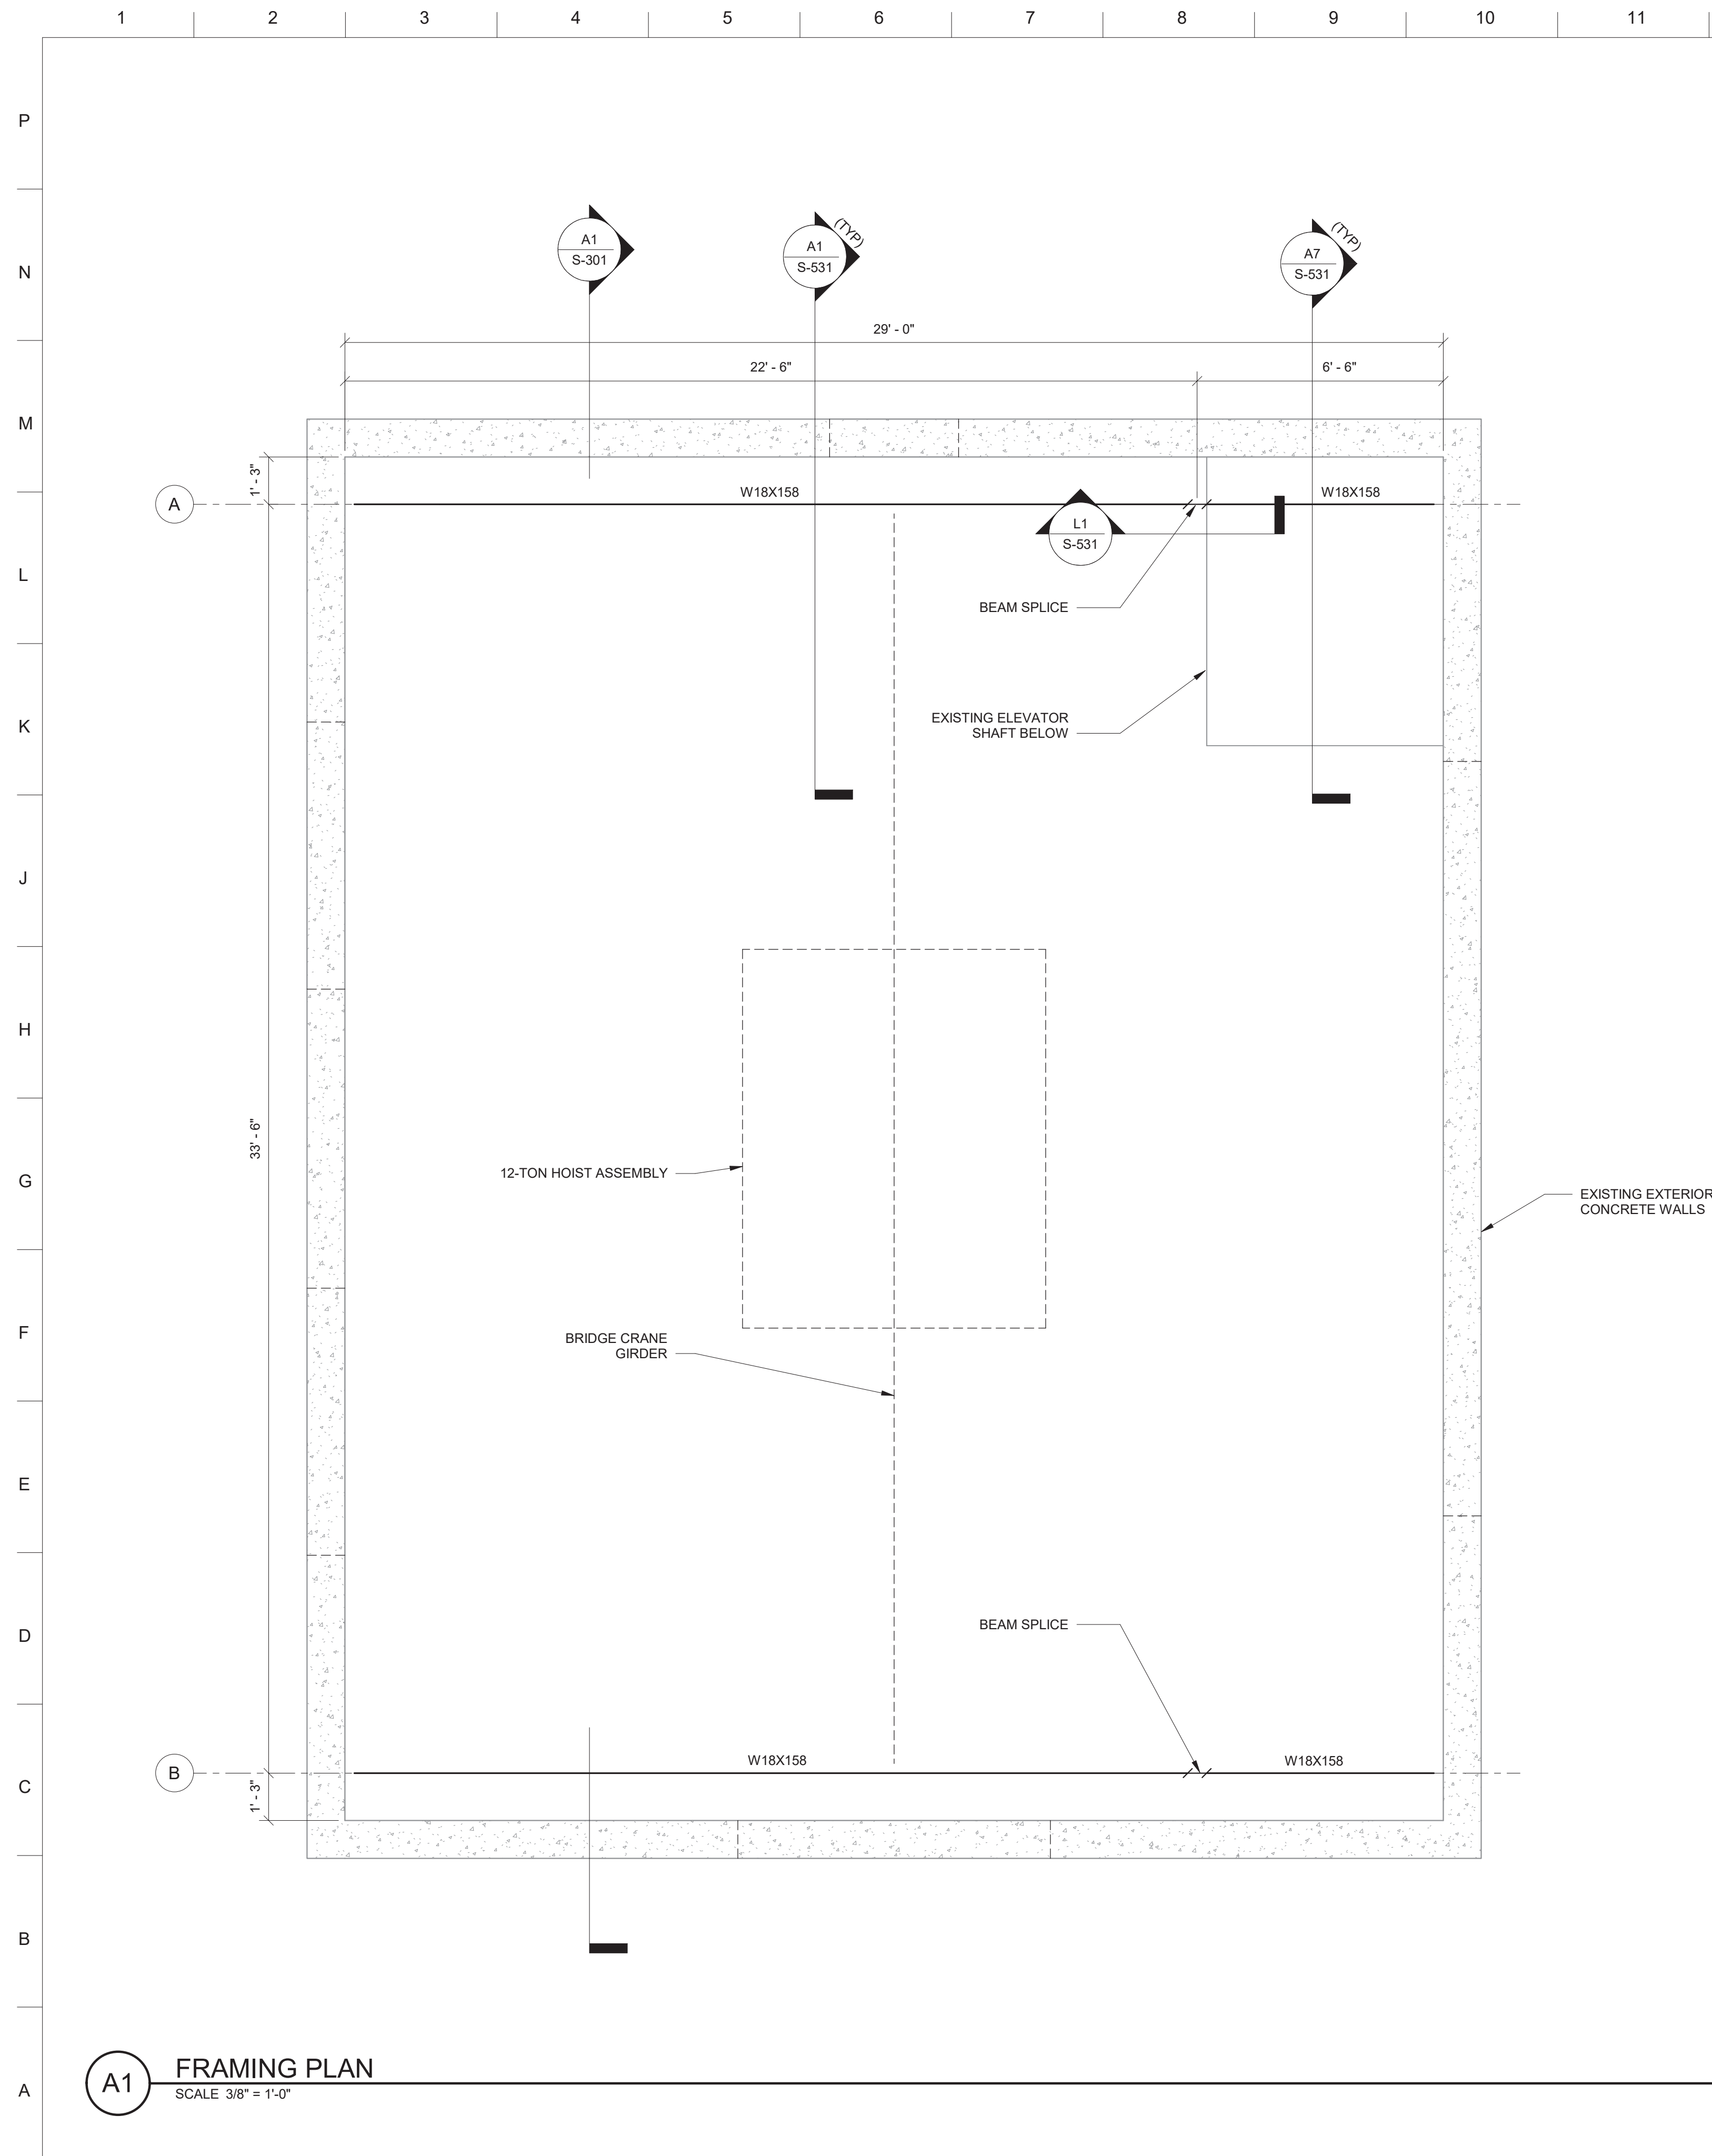

GENERAL SHEET NOTES

1. ALL DIMENSIONS AND ELEVATIONS OF EXISTING ELEMENTS HAVE BEEN PROVIDED TO MATCH THE AS-BUILTS. WORK LIMITS FOR BOTH DEMOLITION AND NEW WORK ARE BETWEEN ELEVATIONS 581' AT THE OPERATING FLOOR TO 607.5' AT THE BOTTOM OF THE ROOF.
2. TOP OF CRANE RAIL MINIMUM ELEVATION = 602' - 6". THE PROVIDED TOP OF CRANE RAIL ELEVATION IS A MINIMUM ELEVATION REQUIRED TO AVOID INTERFERENCES WITH EXISTING EQUIPMENT. THIS ELEVATION CAN BE RAISED IN ORDER TO INCREASE THE TOTAL LIFT HEIGHT BETWEEN THE HOIST HOOK MAX HEIGHT AND THE OPERATING FLOOR.
3. FINAL TOP OF CRANE RAIL ELEVATION TO BE DETERMINED BASED ON FINAL TOTAL HEIGHT OF CRANE RAIL AND CRANE ASSEMBLY. FINAL TOP OF CRANE RAIL ELEVATION MUST BE PROVIDED TO AND APPROVED BY THE CONTRACTING OFFICER PRIOR TO INSTALLATION AND MUST BE REFLECTED IN THE FINAL AS-BUILT DRAWINGS.
4. SEE DETAIL J11/S-531 FOR CRANE RAIL TOLERANCES.
5. MAINTAIN CRANE MANUFACTURER'S MINIMUM CLEARANCES BETWEEN THE CRANE ASSEMBLY, BOTTOM OF ROOF, INTERIOR FACE OF WALLS, AND ANY EXISTING EQUIPMENT. SEE SHEET S-301.
6. TOP OF CRANE GIRDERS AND CRANE GIRDER SUPPORTS TO BE DETERMINED BASED ON FINAL HEIGHT OF CRANE RAIL AND CRANE ASSEMBLY.
7. CRANE SUPPORT BEAMS AND CONNECTION TO EXISTING WALL ARE SUBJECT TO CYCLIC LOADING. FATIGUE IS NOT A DESIGN CONSIDERATION DUE TO THE EXPECTED NUMBER OF CRANE DESIGN LIFE LOADING CYCLES NOT EXCEEDING THE LIMIT FOR FATIGUE DESIGN.
8. EXISTING EQUIPMENT ALONG WALLS AND ON OPERATING FLOOR NOT SHOWN FOR CLARITY. SEE AS-BUILTS FOR EXISTING EQUIPMENT INFORMATION.
9. THE SAFE LOAD CAPACITY OF THE EXISTING OPERATING FLOOR CONCRETE FLOOR SLAB IS 100 PSF DISTRIBUTED LOAD.
10. THE SAFE LOAD CAPACITY OF THE SERVICE BRIDGE IS 40,000 LBS TOTAL. ALL LOADS EXCEEDING 30,000 LBS MUST BE SUBMITTED TO AND APPROVED BY THE CONTRACTING OFFICER PRIOR TO BEING APPLIED TO THE SERVICE BRIDGE.
11. NO VEHICLES, MATERIALS OR EQUIPMENT MAY BE STORED ALONG ANY POINT OF THE SERVICE BRIDGE.
12. NO VEHICLES, MATERIALS, OR EQUIPMENT MAY BE STORED IN A MANNER THAT IMPEDES LAKE OPERATION. SEE SPECIFICATION 00 80 00 00 06 SPECIAL PROVISIONS AND 01 11 00 SUMMARY OF WORK FOR LAKE OPERATION REQUIREMENTS.
13. SEE SHEET S-001 FOR GENERAL NOTES.

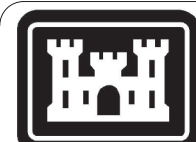

US Army Corps
of Engineers ®

[illegible]

US ARMY CORPS OF ENGINEERS 600 DR. MARTIN LUTHER KING JR. PLACE LOUISVILLE, KY 40202	DESIGNED BY:	Z. HORN	ISSUE DATE:	02/24/2025
	DRAWN BY:	Z. HORN	SOLICITATION NO.:	
	CHECKED BY:	M. WILSON	CONTRACT NO.:	
	SUBMITTED BY:	J. ESTERLE	TED	
	ANSI D			

2150 NOLIN DAM ROAD
MAMMOTH CAVE, KY 42259
NOLIN RIVER LAKE HOIST REPLACEMENT
P2 515776
FRAMING PLAN

SHEET ID


S-111

CERTIFIED FINAL SUBMITTAL W912QR25BA014 Plans-0000

Plot Date: 3/18/2025 2:53:52 PM

File Path:

C:\Temp\515776_v2022_S_Zachary.Lhom.rvt

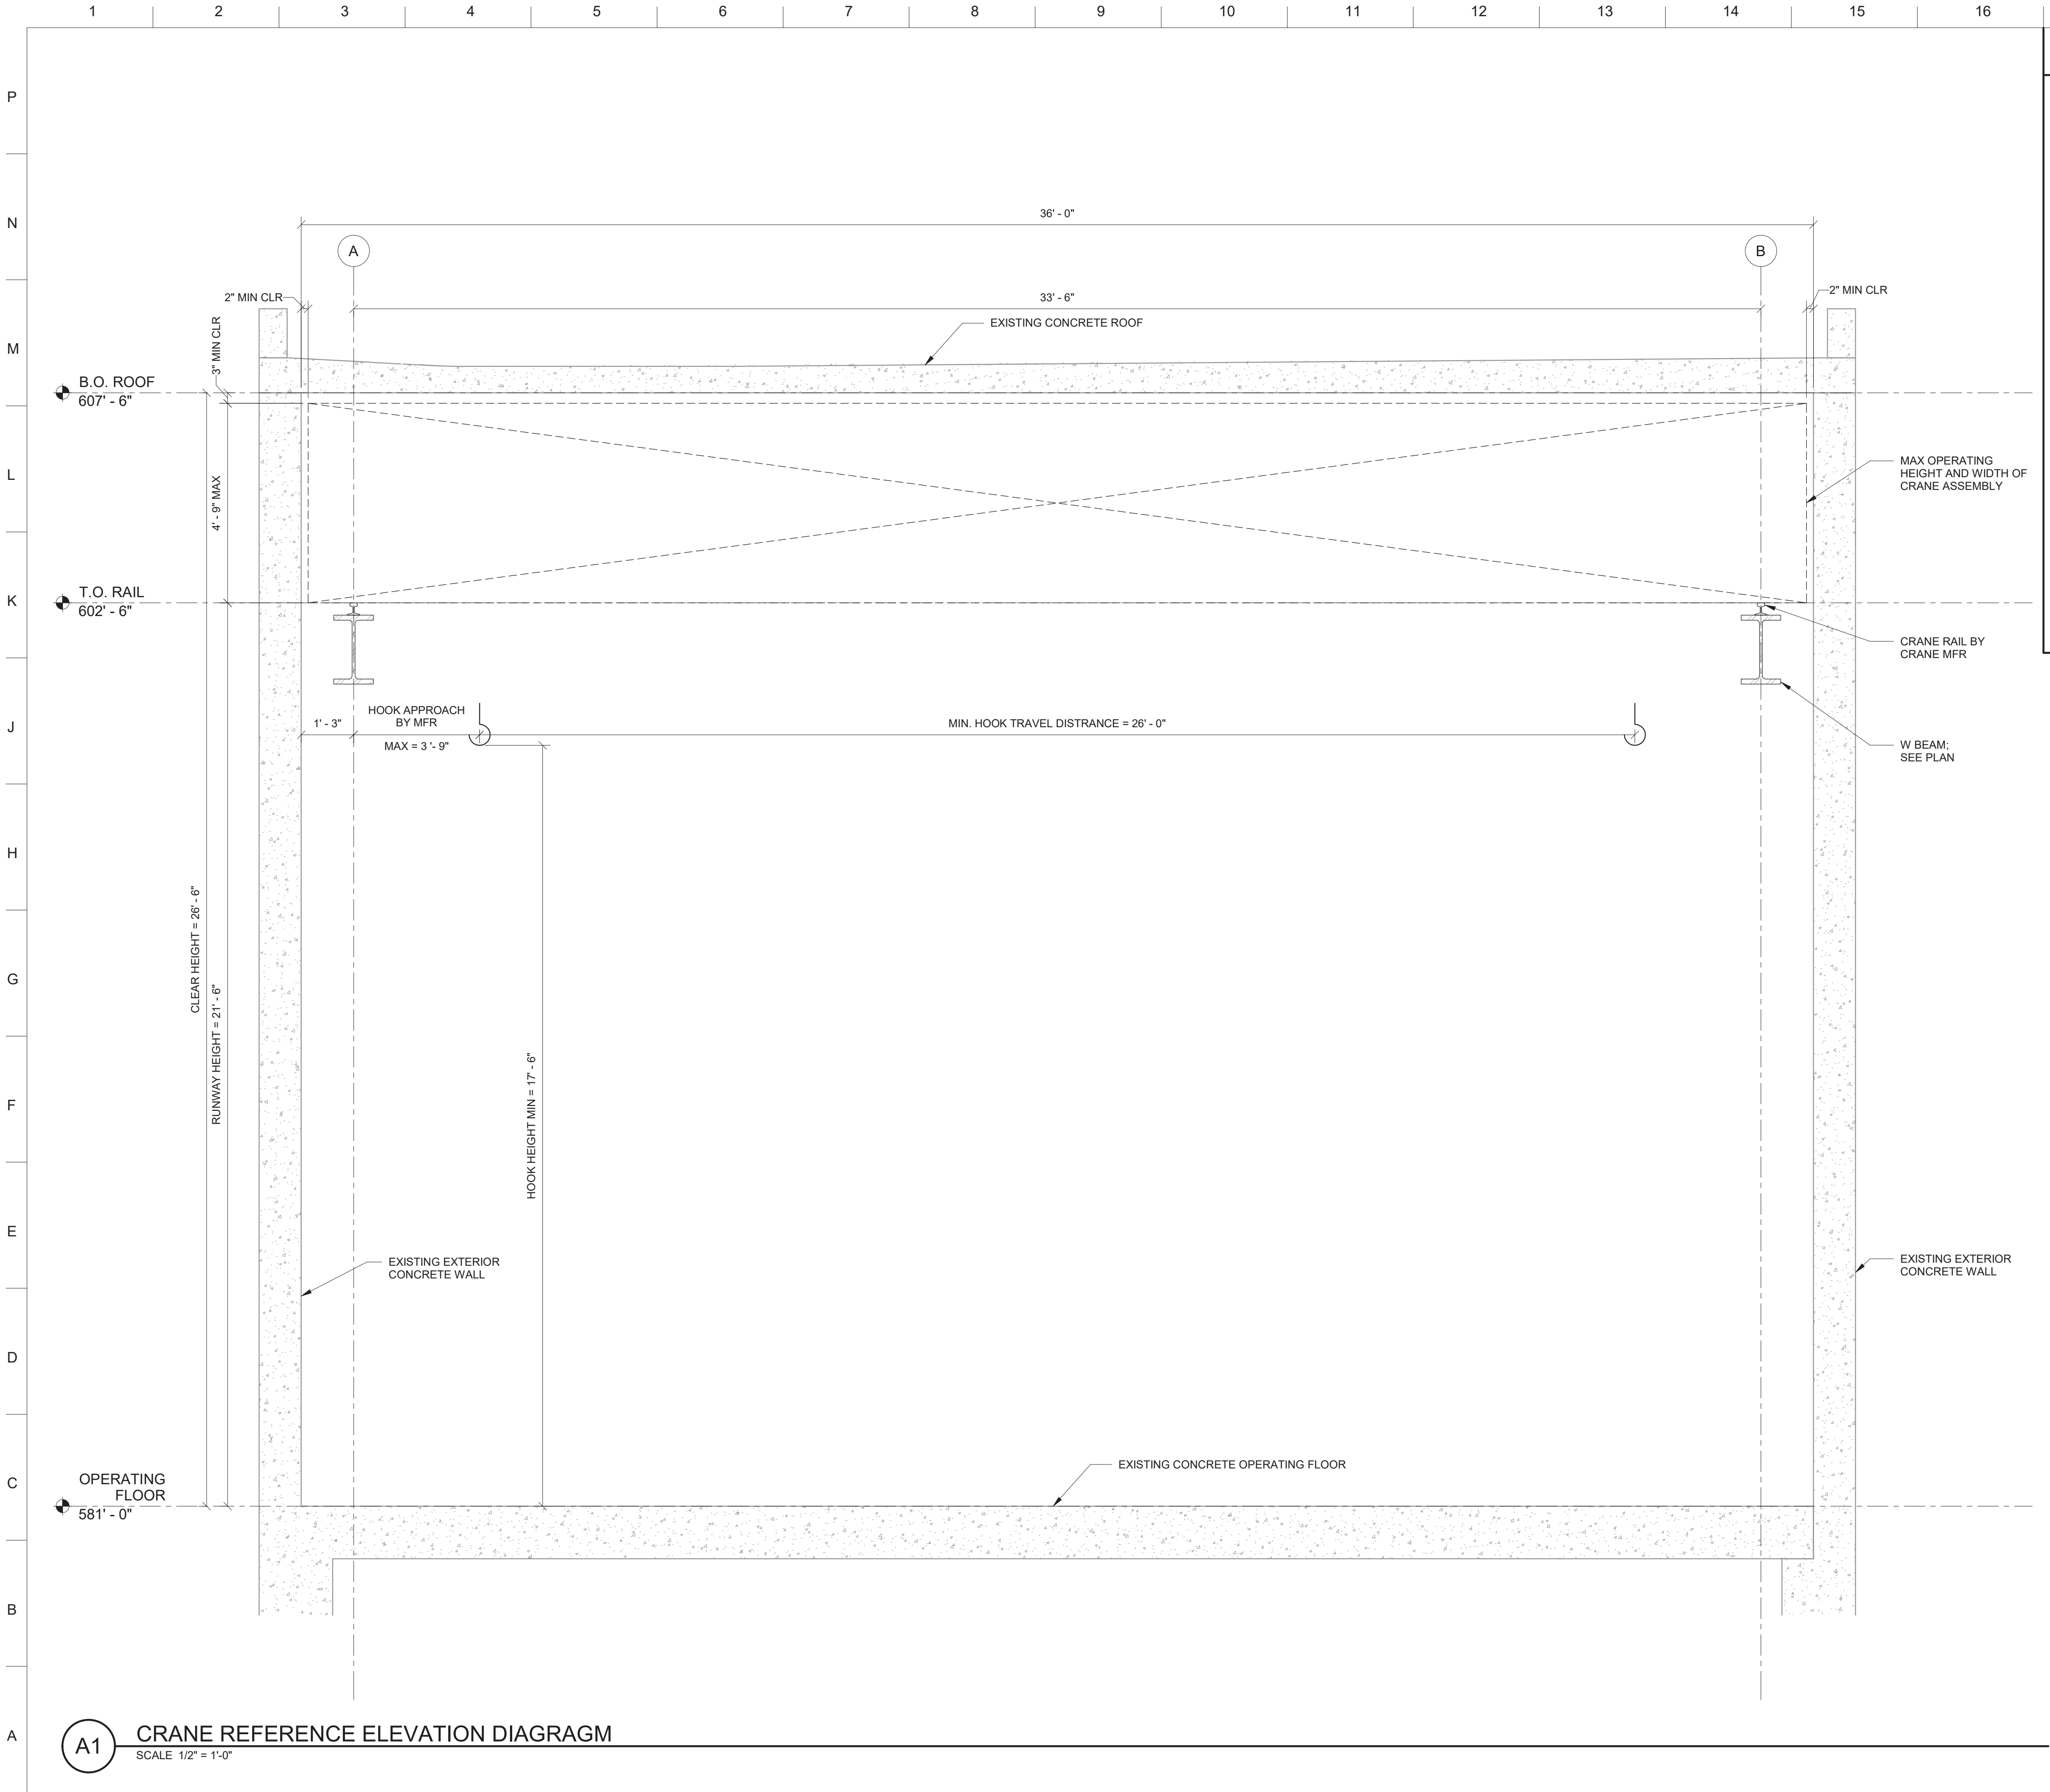

- ### GENERAL SHEET NOTES
- ALL DIMENSIONS AND ELEVATIONS OF EXISTING ELEMENTS HAVE BEEN PROVIDED TO MATCH THE AS-BUILTS. WORK LIMITS FOR BOTH DEMOLITION AND NEW WORK ARE BETWEEN ELEVATIONS 581'-0" AT THE OPERATING FLOOR TO 607'-6" AT THE BOTTOM OF THE ROOF.
 - TOP OF CRANE RAIL MINIMUM ELEVATION = 602' - 6". THE PROVIDED TOP OF CRANE RAIL ELEVATION IS A MINIMUM ELEVATION REQUIRED TO AVOID INTERFERENCES WITH EXISTING EQUIPMENT. THIS ELEVATION CAN BE RAISED IN ORDER TO INCREASE THE TOTAL LIFT HEIGHT BETWEEN THE HOIST HOOK MAX HEIGHT AND THE OPERATING FLOOR.
 - FINAL TOP OF CRANE RAIL ELEVATION TO BE DETERMINED BASED ON FINAL TOTAL HEIGHT OF CRANE RAIL AND CRANE ASSEMBLY. FINAL TOP OF CRANE RAIL ELEVATION MUST BE PROVIDED TO AND APPROVED BY THE CONTRACTING OFFICER PRIOR TO INSTALLATION AND MUST BE REFLECTED IN THE FINAL AS-BUILT DRAWINGS.
 - MINIMUM HOIST LIFT HEIGHT IS 100'.
 - HOOK APPROACH IN PLAN EAST TO WEST DIRECTION BY MANUFACTURER. MAXIMUM HOOK APPROACH IS 5'-0" MEASURED FROM INTERIOR FACE OF EXISTING CONCRETE WALLS TO THE HOOK. REFERENCE AS-BUILTS ATTACHED IN SPECIFICATIONS, SPECIFICALLY DRAWING NUMBER G183-12.142 TO VERIFY CRANE CAN REACH CENTERLINE OF GATE ACCESS HOLES IN THE PLAN NORTH-SOUTH DIRECTION AND DOWNSTREAM SIDE OF GATE ACCESS HOLES IN THE PLAN EAST-WEST DIRECTION.
 - MAINTAIN CRANE MANUFACTURER'S MINIMUM CLEARANCES BETWEEN THE CRANE ASSEMBLY, BOTTOM OF ROOF, INTERIOR FACE OF WALLS, AND ANY EXISTING EQUIPMENT.
 - TOP OF CRANE GIRDERS AND CRANE GIRDER SUPPORTS TO BE DETERMINED BASED ON FINAL HEIGHT OF CRANE RAIL AND CRANE ASSEMBLY.
 - EXISTING EQUIPMENT ALONG WALLS AND ON OPERATING FLOOR NOT SHOWN FOR CLARITY. SEE AS-BUILTS AND SD-111 FOR ADDITIONAL EXISTING EQUIPMENT INFORMATION.
 - IT IS EXPECTED THAT THE ELEVATOR SHAFT EQUIPMENT, LADDER, FLUME AND EXHAUST PIPES WILL NOT CONFLICT WITH THE RAIL OR BRIDGE CRANE. VERIFY MAX OBSTRUCTION DISTANCE IN FIELD. SEE AS-BUILTS AND SD-111 FOR ADDITIONAL EXISTING EQUIPMENT INFORMATION.
 - SEE SHEET S-001 FOR GENERAL NOTES.



MARK	DESCRIPTION	DATE

DESIGNED BY: Z. HORN	ISSUE DATE: 02-24-2025
DRAWN BY: E. GARCIA	SOLICITATION NO.: TED
CHECKED BY: M. WILSON	CONTRACT NO.: TED
SUBMITTED BY: J. ESTERLE	
SIZE: ANSI D	

US ARMY CORPS OF ENGINEERS LOUISVILLE DISTRICT 600 DR. MARTIN LUTHER KING JR. PLACE LOUISVILLE, KY 40202	
---	--

2150 NOLIN DAM ROAD MAMMOTH CAVE, KY 42259 NOLIN RIVER LAKE HOIST REPLACEMENT P2 515776 CRANE REFERENCE DIAGRAM

SHEET ID S-301



SCALE 1/2" = 1'-0"



NOTE: CRANE MUST NOT BE PRESENT IN THE PORTION OF RUNWAY BEING MEASURED. INTERACTION BETWEEN THE CRANE AND RUNWAY MUST NOT BE USED TO ACHIEVE RUNWAY TOLERANCES.

SCALE: NTS



SCALE 3/4" = 1'-0"



--	--	

