

TITLE SHEET

ROADS/PAVEMENTS & MISC. CIVIL WORK
IDIQ CONTRACT

MISAWA AIR BASE
JAPAN

1-May-26

Solicitation No.
Contract No.

PREPARED BY:
35 CIVIL ENGINEERING SQUADRON
US AIR FORCE, MISAWA AB
APO AP 96319-5022

	PROJECT TITLE:	RF.NO.	SHEET NUMBER			SEQ.NO.
DRAWING BY: NH	ROADS/PAVEMENTS & MISC. CIVIL WORK IDIQ CONTRACT		CLASS	LOG	SHEET	
CHECKED BY: NH	TITLE SHEET	T-1			1 OF 18	1

LIST OF DRAWINGS

SEQ. NO.	SHEET NO.	REF.NO.	DESCRIPTION	DATE OF DRAWING/REVISION
1	1 OF 18	T-1	TITLE SHEET	
2	2 OF 18	T-2	LIST OF DRAWINGS	
3	3 OF 18	T-3	REVISIONS	
4	4 OF 18	T-4	LOCATION MAP	
5	5 OF 18	T-5	LOCATION MAP (MFH AREA)	
6	6 OF 18	T-6	LOCATION MAP (MFH AREA)	
7	7 OF 18	C-1	CRACK REPAIR DETAIL (GEOTEXTILE)	
8	8 OF 18	C-2	CONCRETE SIDEWALK DETAIL	
9	9 OF 18	C-3	CONCRETE CURBS DETAIL	
10	10 OF 18	C-4	CONCRETE CURBS & GUTTER DETAIL	
11	11 OF 18	C-5	ALPHANUMERIC SYMBOL DETAIL	
12	12 OF 18	C-6	HANDICAP PAVEMENT MARKINGS	
13	13 OF 18	C-7	STANDARD EARTHWORKS FOR PIPE	
14	14 OF 18	C-8	GUTTER INLET DETAIL	
15	15 OF 18	C-9	BOX CULVERT DETAIL	
16	16 OF 18	C-10	MANHOLE DETAIL	
17	17 OF 18	C-11	BOLLARD SLEEVE	
18	18 OF 18	C-11	CONSTRUCTION SIGN	


	PROJECT TITLE:	RF.NO.	SHEET NUMBER			SEQ.NO.
DRAWING BY: NH	ROADS/PAVEMENTS & MISC. CIVIL WORK IDIQ CONTRACT		CLASS	LOG	SHEET	
CHECKED BY: NH	LIST OF DRAWINGS	T-2			2 OF 18	2

REVISIONS

[illegible]





Project location is entire Misawa Air Base and locations within 40 km radius from Misawa AB, including its associated sites of Fleet Logistics Center Yokosuka Hachinohe Fuel Terminal, with the exception of the Misawa AB Airfield and Draughton Range.,

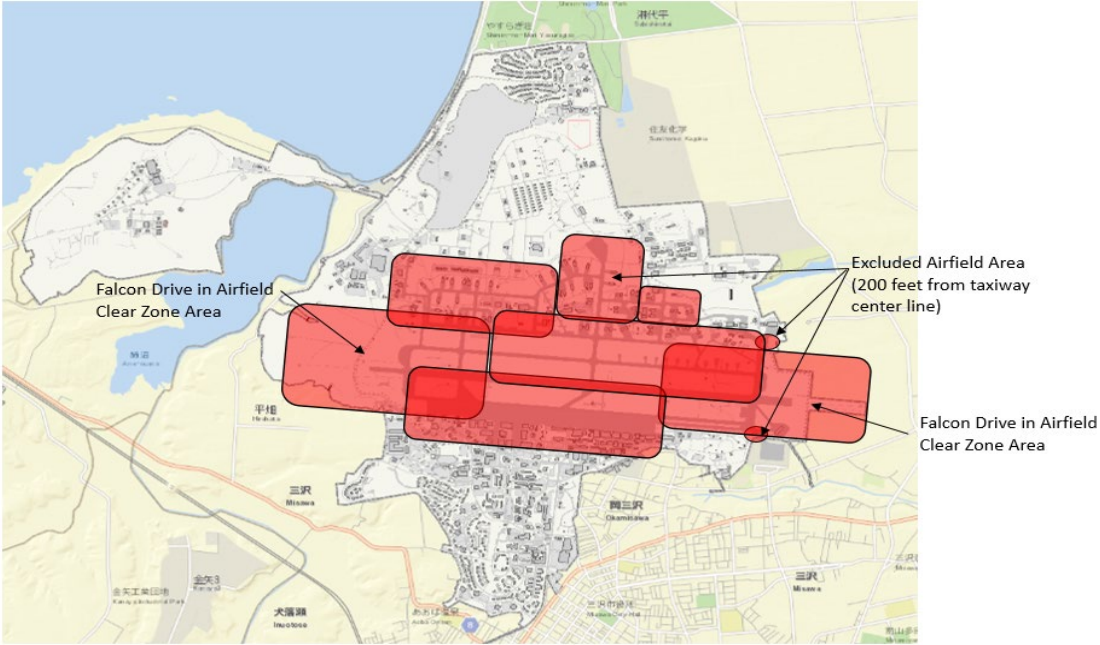

LOCATION MAP OF MISAWA AB

	PROJECT TITLE:	RF.NO.	SHEET NUMBER			SEQ.NO.
DRAWING BY: NH	ROADS/PAVEMENTS & MISC. CIVIL WORK IDIQ CONTRACT		CLASS	LOG	SHEET	
CHECKED BY: NH	LOCATION MAP	T-4			4 OF 18	4


Location Map for Main Base MFH

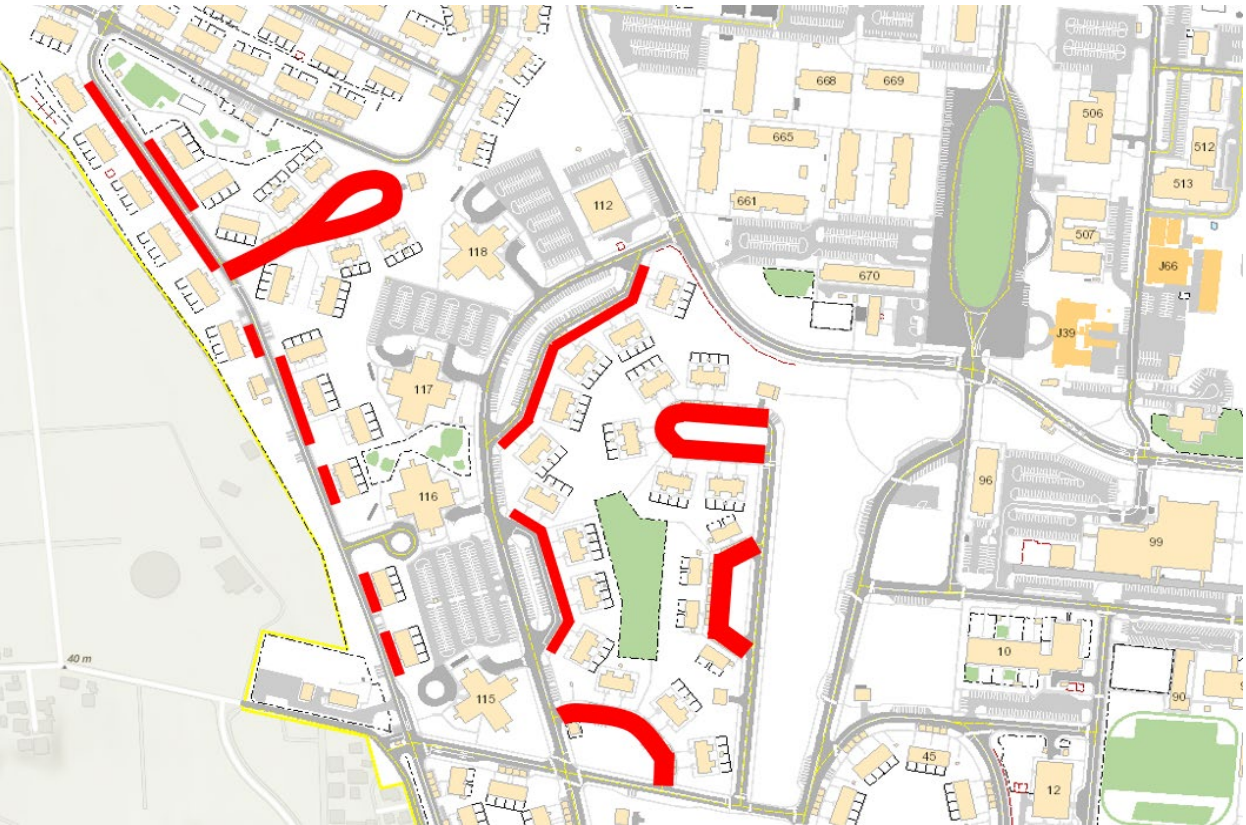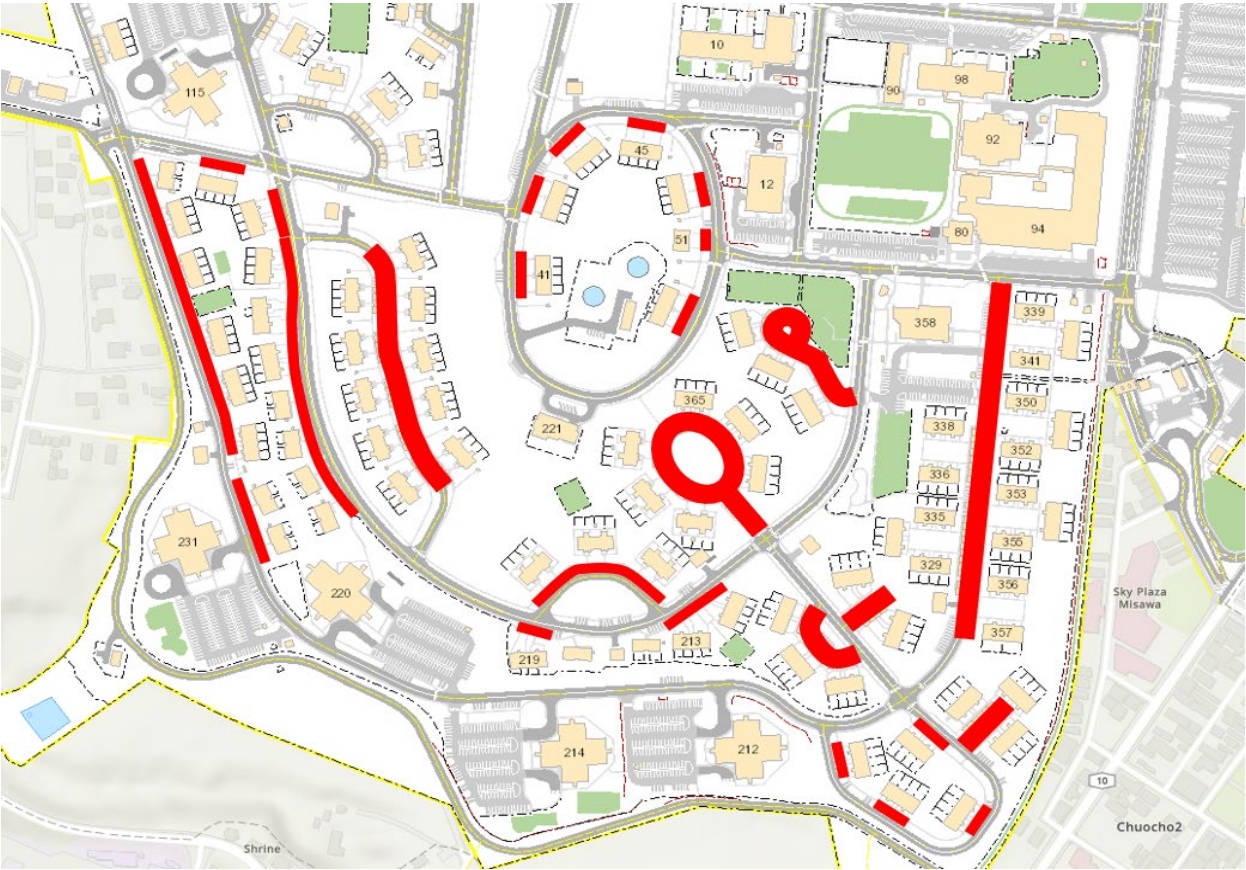


MFH Carport Areas include the streets, sidewalks and areas under the carports, as indicated in the red lines (ref. Specifications Section 01 11 00, para. 1.1.1.12 thru 1.1.1.16). For the streets not indicated in the red lines, Specifications Section 01 11 00, para. 1.1.1.1 thru 1.1.1.11 applies.

	PROJECT TITLE:	RF.NO.	SHEET NUMBER			SEQ.NO.
DRAWING BY: NH	ROADS/PAVEMENTS & MISC. CIVIL WORK IDIQ CONTRACT		CLASS	LOG	SHEET	
CHECKED BY: NH	LOCATION MAP (MFH AREA)	T-5			5 OF 18	5

Location Map for Main Base MFH

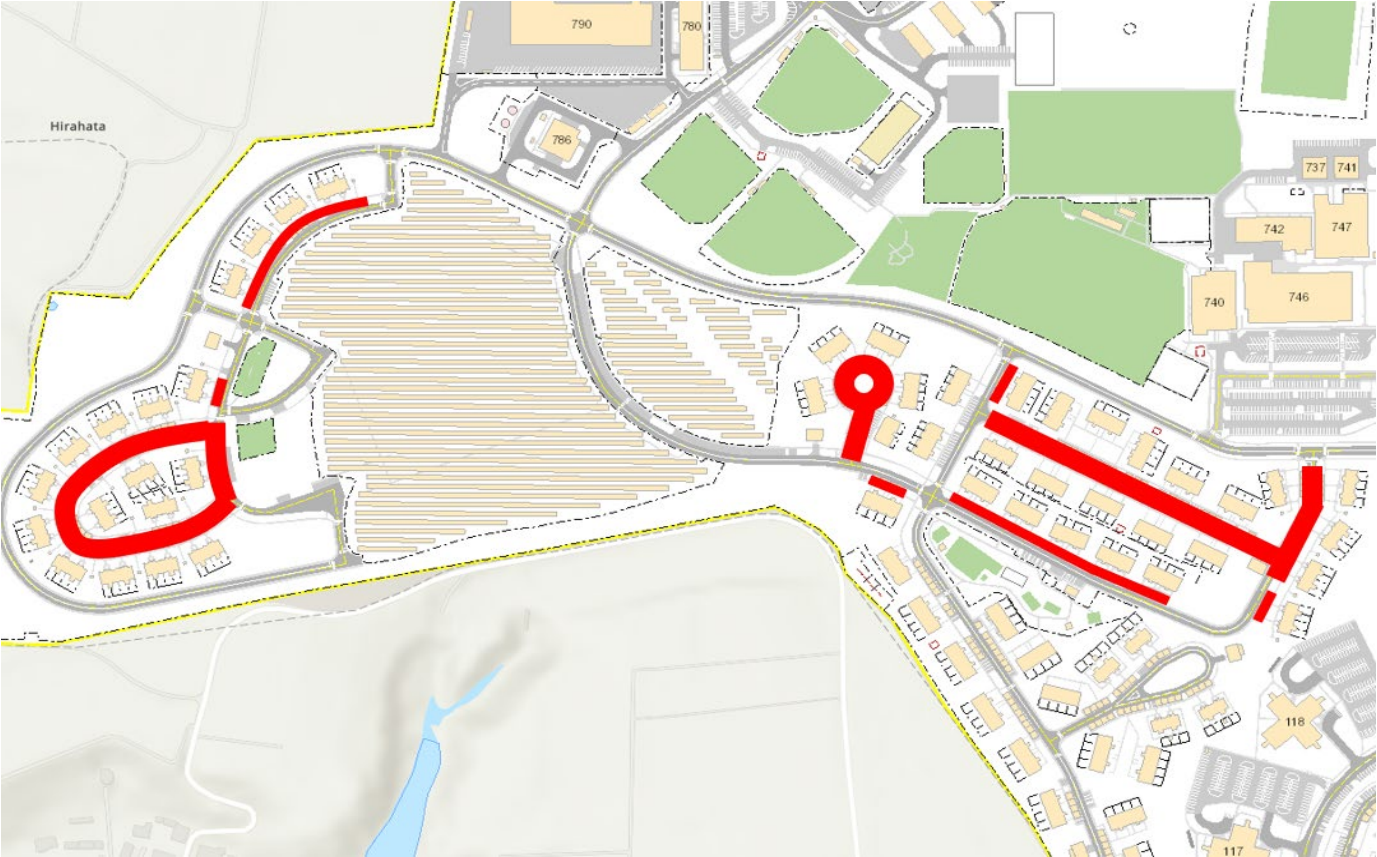


Location Map for North Base MFH

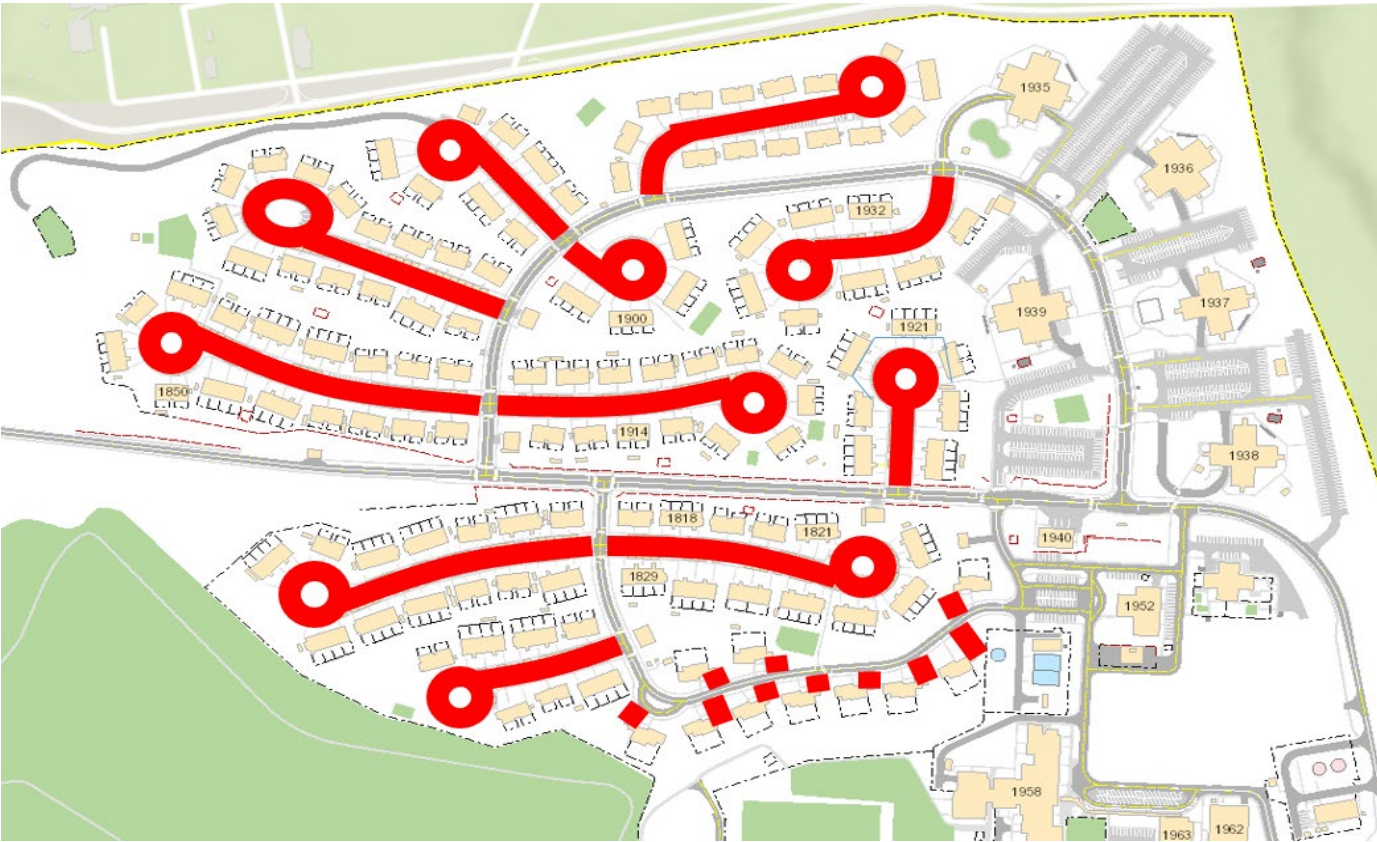

MFH Carport Areas include the streets, sidewalks and areas under the carports, as indicated in the red lines (ref. Specifications Section 01 11 00, para. 1.1.1.12 thru 1.1.1.16). For the streets not indicated in the red lines, Specifications Section 01 11 00, para. 1.1.1.1 thru 1.1.1.11 applies.

PROJECT TITLE:		RF.NO.	SHEET NUMBER			SEQ.NO.
DRAWING BY: NH	ROADS/PAVEMENTS & MISC. CIVIL WORK IDIQ CONTRACT	T-6	CLASS	LOG	SHEET	6
CHECKED BY: NH	LOCATION MAP (MFH AREA)				6 OF 18	

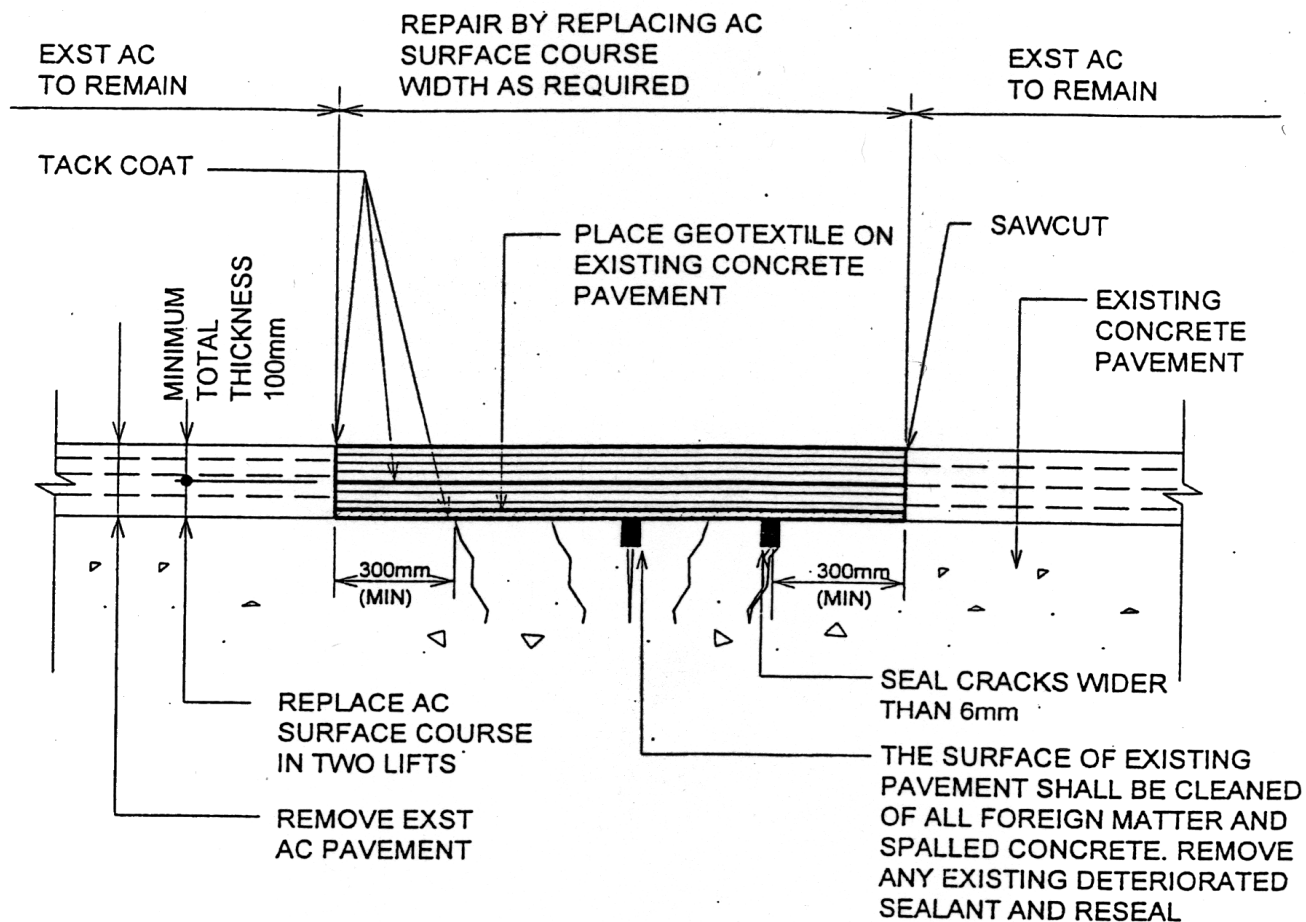


NOTE:

1. THICKNESS OF EXISTING AC SURFACE SHALL BE VERIFIED IN THE FIELD.
2. GEOTEXTILE SHALL EXTEND A MINIMUM 300MM BEYOND CRACK.
3. CRACKS WIDTH LESS THAN 20MM SHALL BE FIELD WITH JOINT SEALANT. CRACKS WIDTH LARGER THAN 20MM SHALL BE FILLED WITH A BITUMINOUS MIXTURE OF SAND AND ASPHALT.

CRACK REPAIR DETAIL (GEOTEXTILE)

	PROJECT TITLE:	RF.NO.	SHEET NUMBER			SEQ.NO.
DRAWING BY: NH	ROADS/PAVEMENTS & MISC. CIVIL WORK IDIQ CONTRACT		CLASS	LOG	SHEET	
CHECKED BY: NH	CRACK REPAIR DETAIL (GEOTEXTILE)	C-1			7 OF 18	7

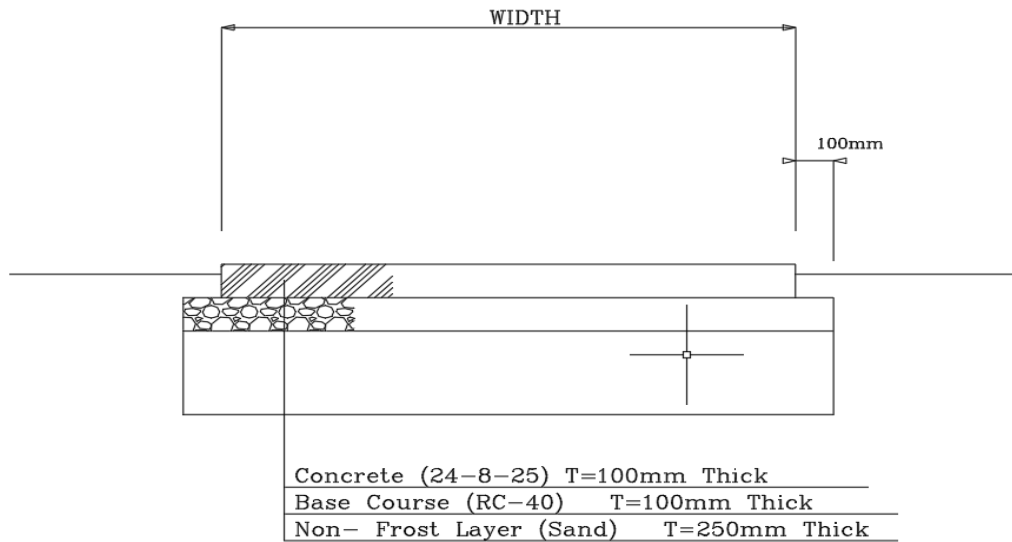


SECTION


NOTES:

1. TRANSVERSE CONTRACTION JOINTS SHALL BE LOCATED SUCH THAT THE LENGTH DIMENSION OF THE SLABS IS NO GREATER THAN 1.25 TIMES THE WIDTH AND NORMALLY 1.0 TIMES THE WIDTH.

2. EXPANSION JOINTS SHALL BE CONSTRUCTED NOT MORE THAN FIVE TIMES THE WIDTH "W" OF THE WALKWAY.

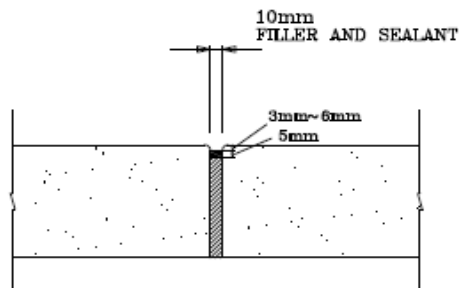


EXPANTION JOINT

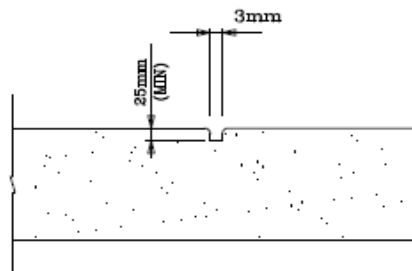


TRANSVERSE CONTRACTION JOINT

CONCRETE SIDEWALK DETAIL

	PROJECT TITLE:	RF.NO.	SHEET NUMBER			SEQ.NO.
DRAWING BY: NH	ROADS/PAVEMENTS & MISC. CIVIL WORK IDIQ CONTRACT		CLASS	LOG	SHEET	
CHECKED BY: NH	CONCRETE SIDEWALK DETAIL	C-2			8 OF 18	8

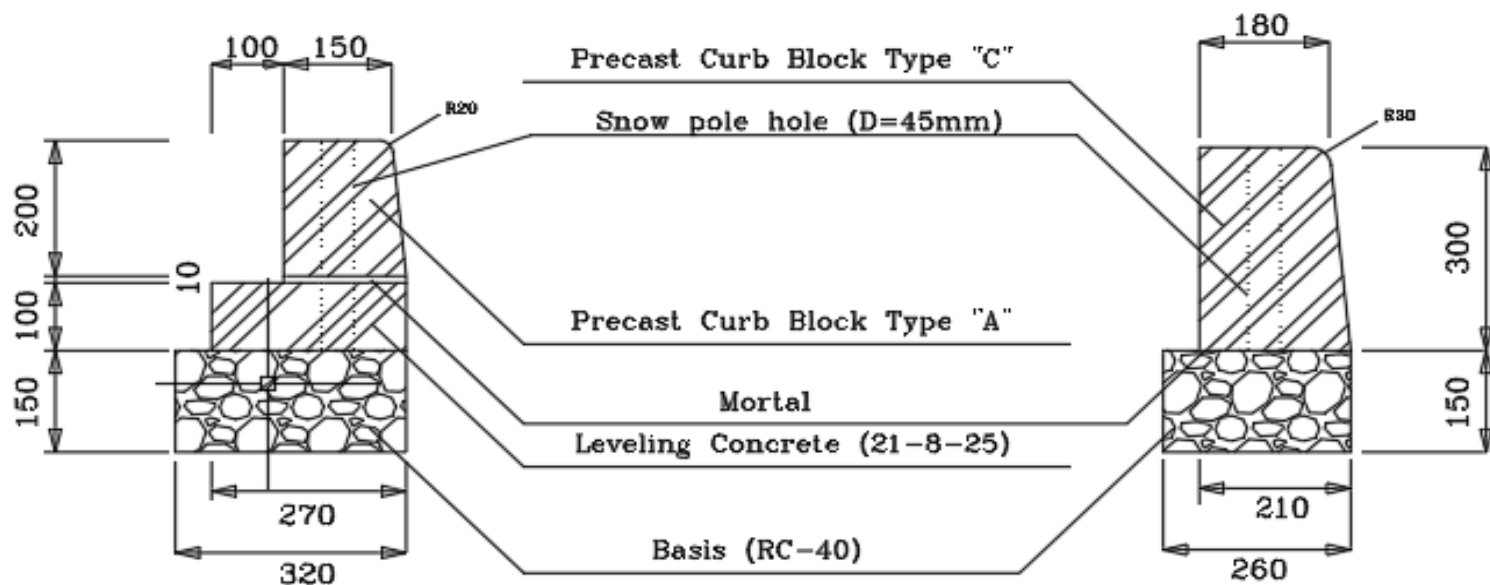


PRECAST CONCRETE CURB BLOCK TYPE A & TYPE C

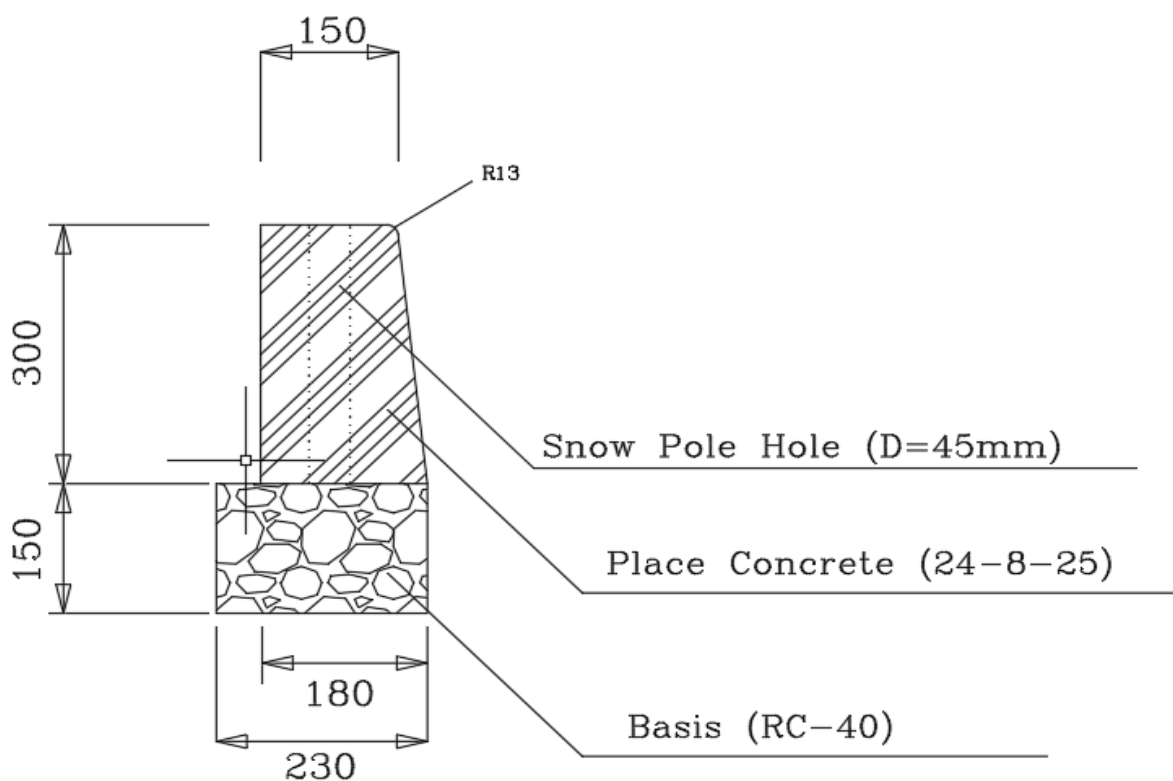



CAST-IN PLACE CONCRETE CURB 150 MM (BARRIER)

CONCRETE CURBS DETAIL

	PROJECT TITLE:	RF.NO.	SHEET NUMBER			SEQ.NO.
DRAWING BY: NH	ROADS/PAVEMENTS & MISC. CIVIL WORK IDIQ CONTRACT		CLASS	LOG	SHEET	
CHECKED BY: NH	CONCRETE CURBS DETAIL	C-3			9 OF 18	9

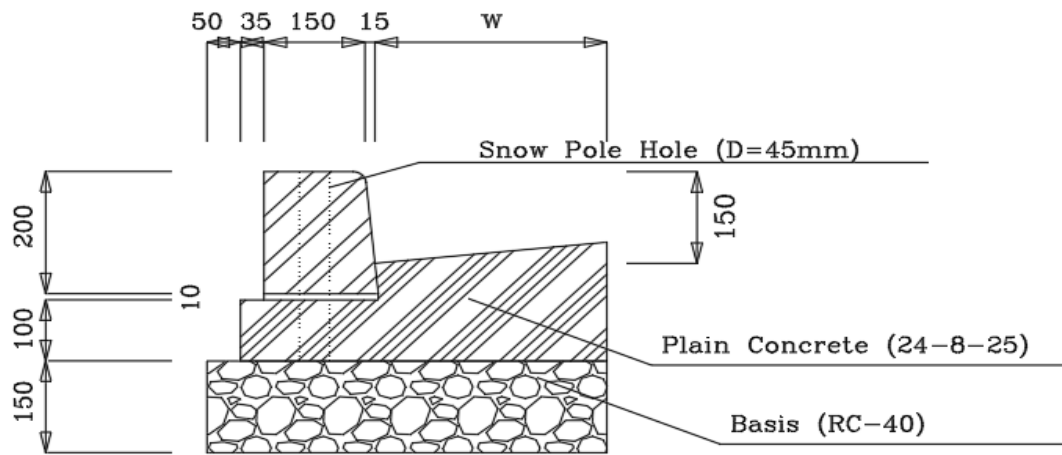


PRECAST A BLOCK & CAST-IN PLACE CONCRETE GUTTER

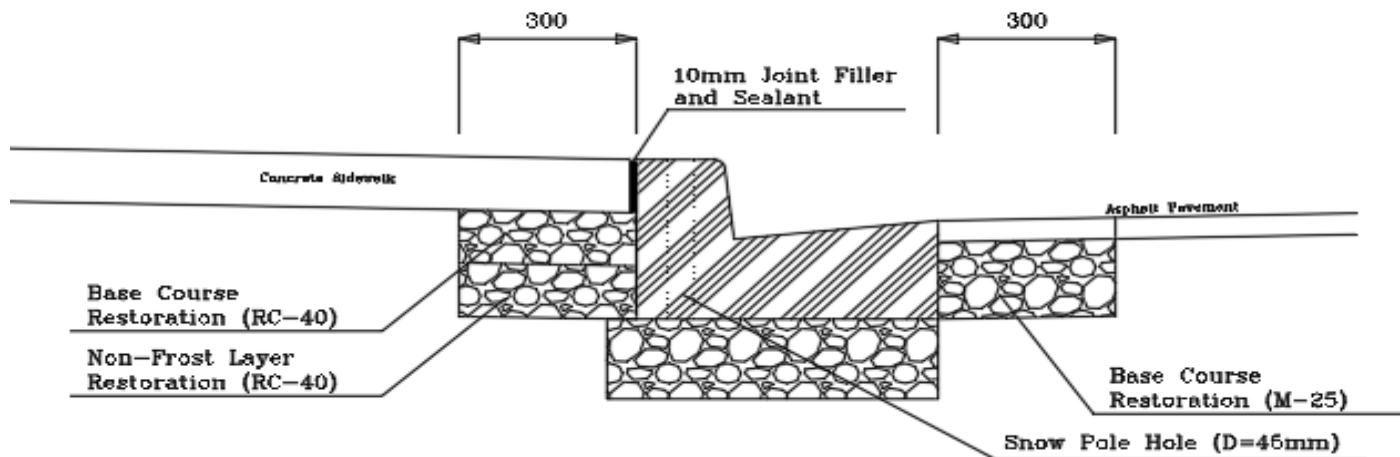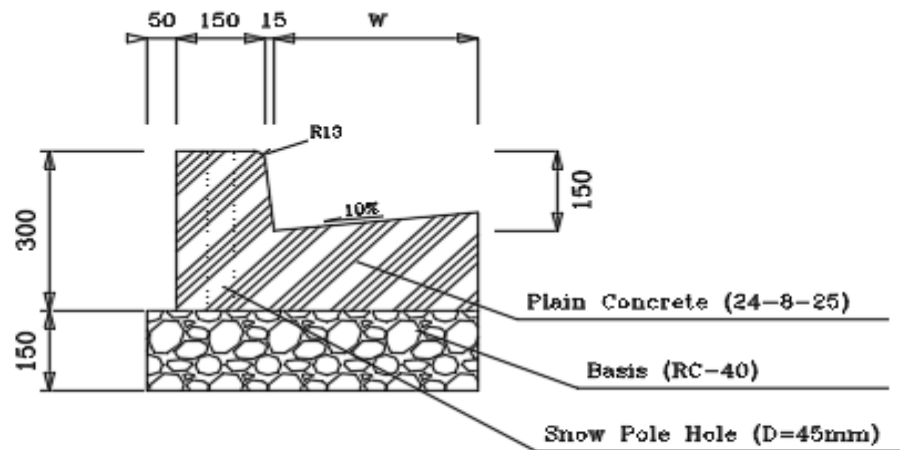

CAST-IN PLACE STANDARD BARRIER CONCRETE CURB AND GUTTER

CONCRETE CURBS & GUTTER DETAIL

	PROJECT TITLE:	RF.NO.	SHEET NUMBER			SEQ.NO.
DRAWING BY: NH	ROADS/PAVEMENTS & MISC. CIVIL WORK IDIQ CONTRACT		CLASS	LOG	SHEET	
CHECKED BY: NH	CONCRETE CURBS & GUTTER DETAIL	C-4			10 OF 18	10

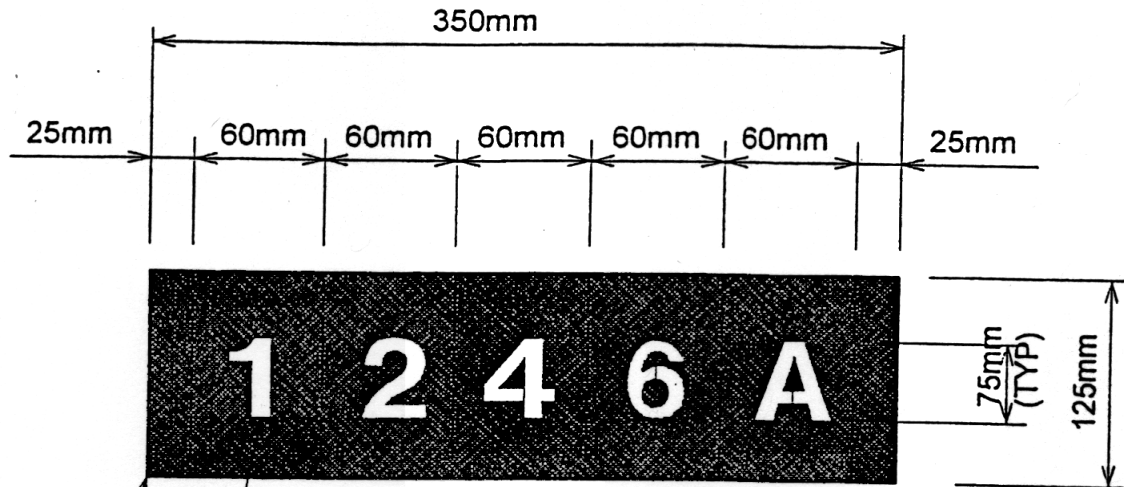

WHITE BLOCK STYLE LETTERING

BROWN BACK GROUND (350mm x 125mm)
NUMBER OF SYMBOLS VARIES FROM 3 TO 5
(TYPICAL), CENTERED ON WHITE BACK
GROUND

ALPHANUMERIC SYMBOL DETAIL

	PROJECT TITLE:	RF.NO.	SHEET NUMBER			SEQ.NO.
DRAWING BY: NH	ROADS/PAVEMENTS & MISC. CIVIL WORK IDIQ CONTRACT		CLASS	LOG	SHEET	
CHECKED BY: NH	ALPHANUMERIC SYMBOL DETAIL	C-5			11 OF 18	11

The diagram shows the orthographic projection of a mechanical part, consisting of a front view (top) and a top view (bottom).

Front View (Top):


- Overall height: 1080
- Top horizontal segment width: 180
- Radius of the top fillet: R150
- Thickness of the part: 60
- Horizontal distance from the left edge to the center of the circular feature: 1500

Top View (Bottom):

- Overall width: 1500
- Radius of the circular feature: R600
- Horizontal distance from the center of the circular feature to the start of the horizontal segment: 450
- Thickness of the part: 60
- Horizontal distance from the right edge to the end of the horizontal segment: 450
- Vertical distance from the horizontal centerline to the top edge of the horizontal segment: 130
- Vertical distance from the horizontal centerline to the bottom edge of the horizontal segment: 150

HANDICAP PAVEMENT MARKINGS

	PROJECT TITLE:	RF.NO.	SHEET NUMBER			SEQ.NO.
DRAWING BY: NH	ROADS/PAVEMENTS & MISC. CIVIL WORK IDIQ CONTRACT	C-6	CLASS	LOG	SHEET	12
CHECKED BY: NH	HANDICAP PAVEMENT MARKINGS				12 OF 18	

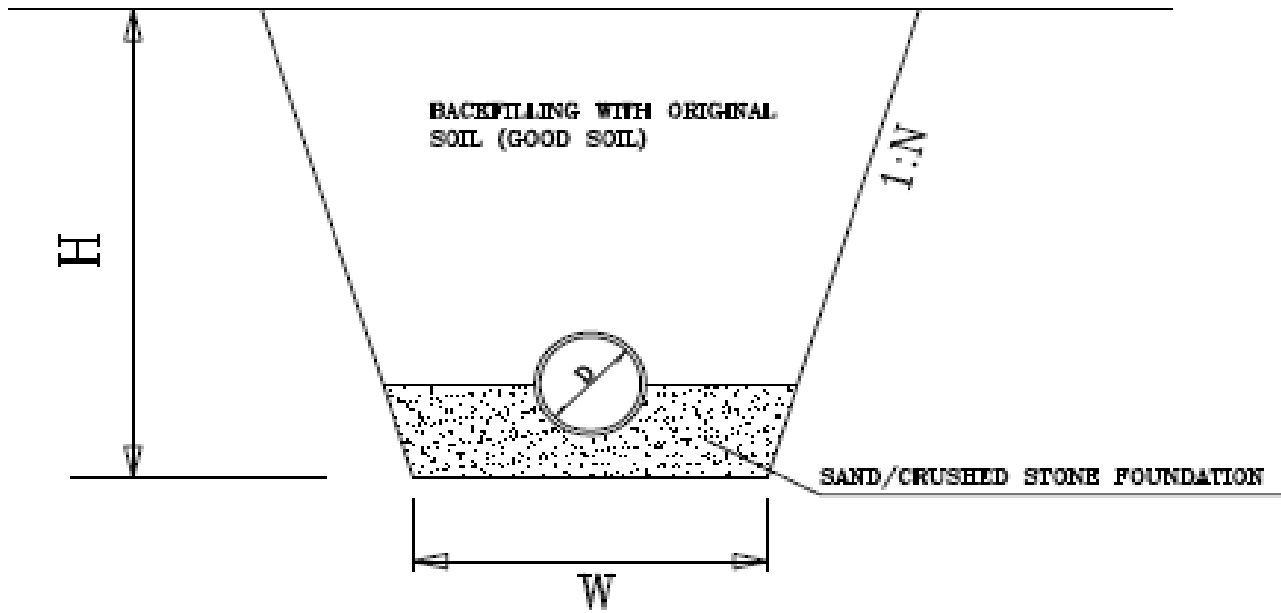

D	LESS THAN 150mm	200~300	350	400	450	500 or more
W	700 (500)	700 (800)	700	800	900	D+500


NOTE: THE VALUES IN () SHOULD BE TAKEN IN CASE RECAVATION WORK IS DONE MAN POWER.

RECAVATION SLOPE

H	N
$H < 1m$	STRAIGHT
$1m < H < 3m$	0.3
$3m < H < 5m$	0.5

STANDARD EARTHWORKS FOR PIPE



	PROJECT TITLE:	RF.NO.	SHEET NUMBER			SEQ.NO.
DRAWING BY: NH	ROADS/PAVEMENTS & MISC. CIVIL WORK IDIQ CONTRACT		CLASS	LOG	SHEET	
CHECKED BY: NH	STANDARD EARTHWORKS FOR PIPE	C-7			13 OF 18	13

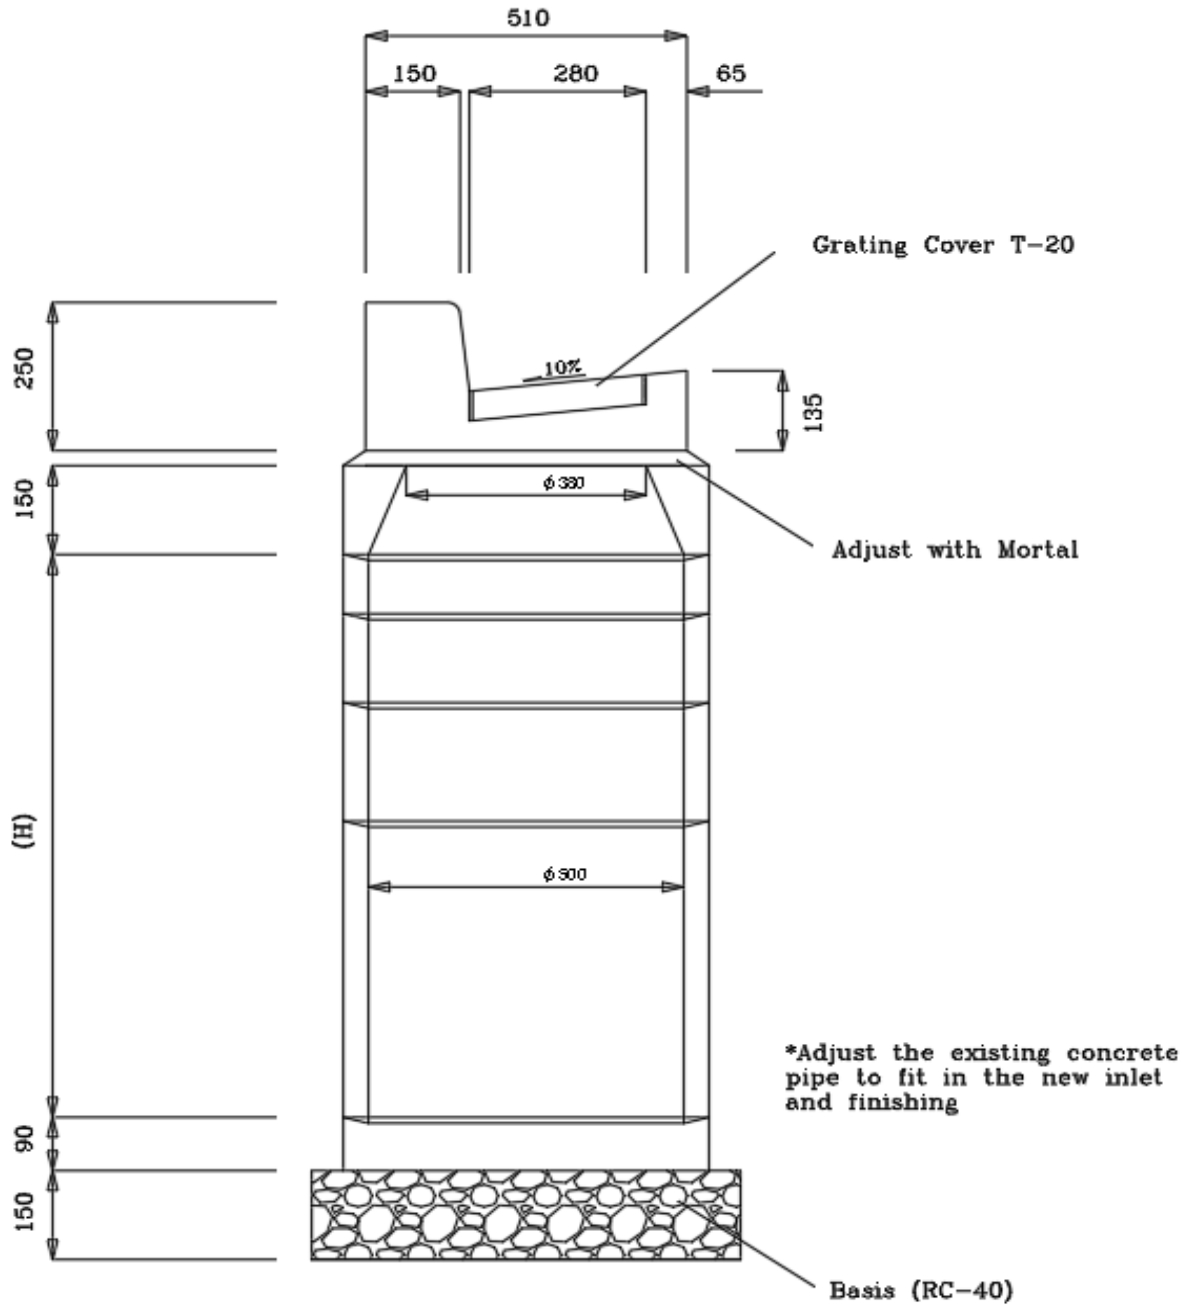

Unit: mm

GUTTER INLET DETAIL



	PROJECT TITLE:	RF.NO.	SHEET NUMBER			SEQ.NO.
DRAWING BY: NH	ROADS/PAVEMENTS & MISC. CIVIL WORK IDIQ CONTRACT		CLASS	LOG	SHEET	
CHECKED BY: NH	GUTTER INLET DETAIL	C-8			14 OF 18	14

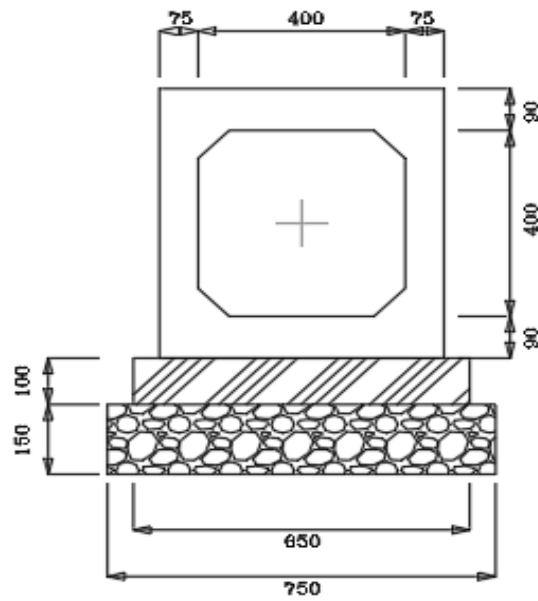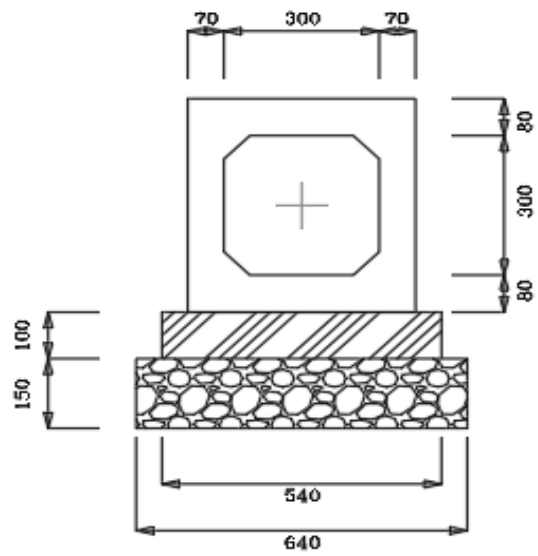

Unit: mm

BOX CULVERT DETAIL


	PROJECT TITLE:	RF.NO.	SHEET NUMBER			SEQ.NO.
DRAWING BY: NH	ROADS/PAVEMENTS & MISC. CIVIL WORK IDIQ CONTRACT		CLASS	LOG	SHEET	
CHECKED BY: NH	BOX CULVERT DETAIL	C-9			15 OF 18	15

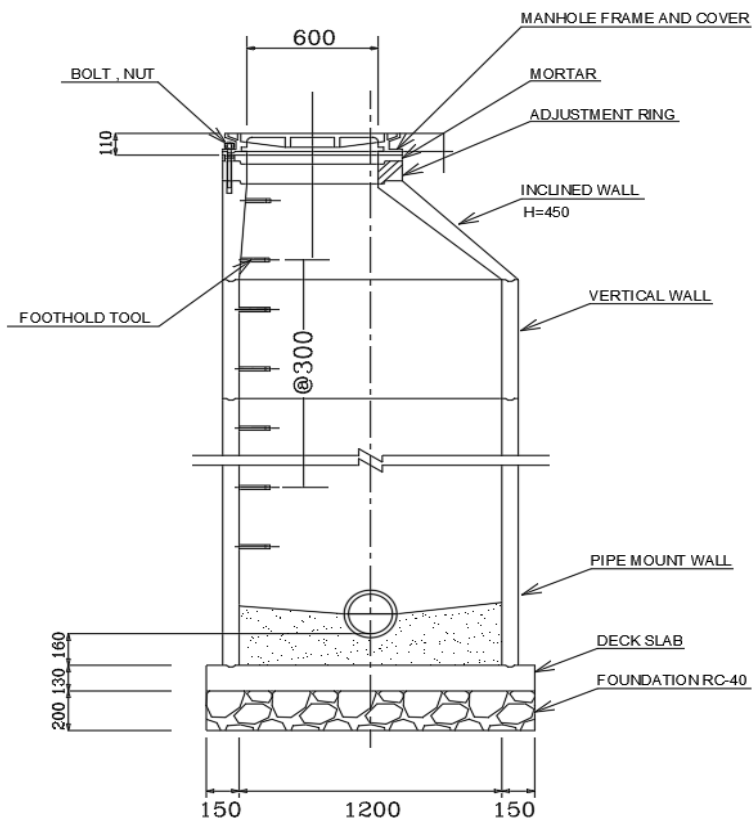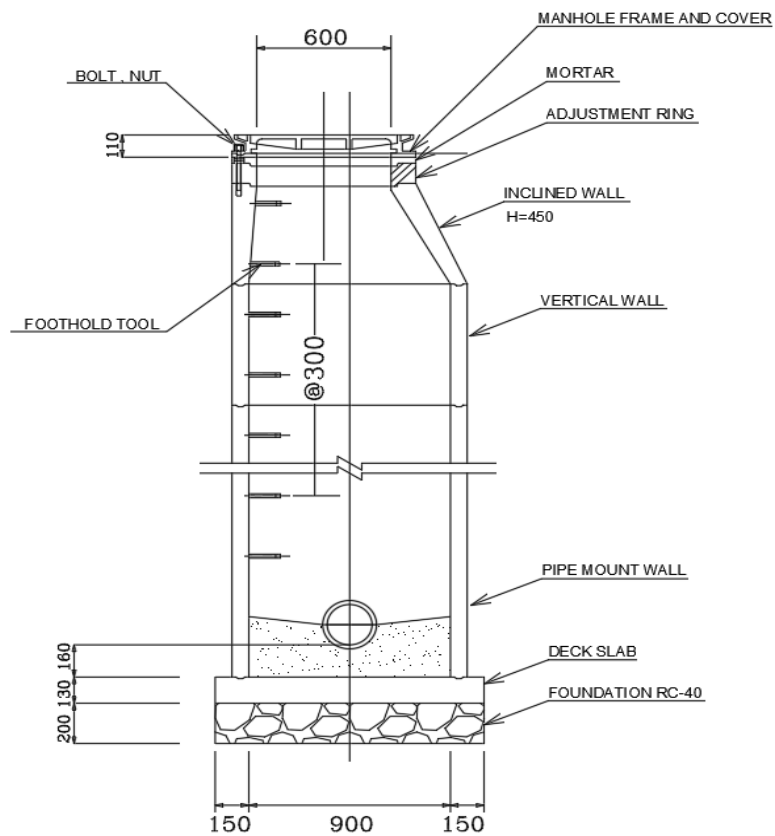

Unit: mm

MANHOLE DETAIL

	PROJECT TITLE:	RF.NO.	SHEET NUMBER			SEQ.NO.
DRAWING BY: NH	ROADS/PAVEMENTS & MISC. CIVIL WORK IDIQ CONTRACT		CLASS	LOG	SHEET	
CHECKED BY: NH	MANHOLE DETAIL	C-10			16 OF 18	16

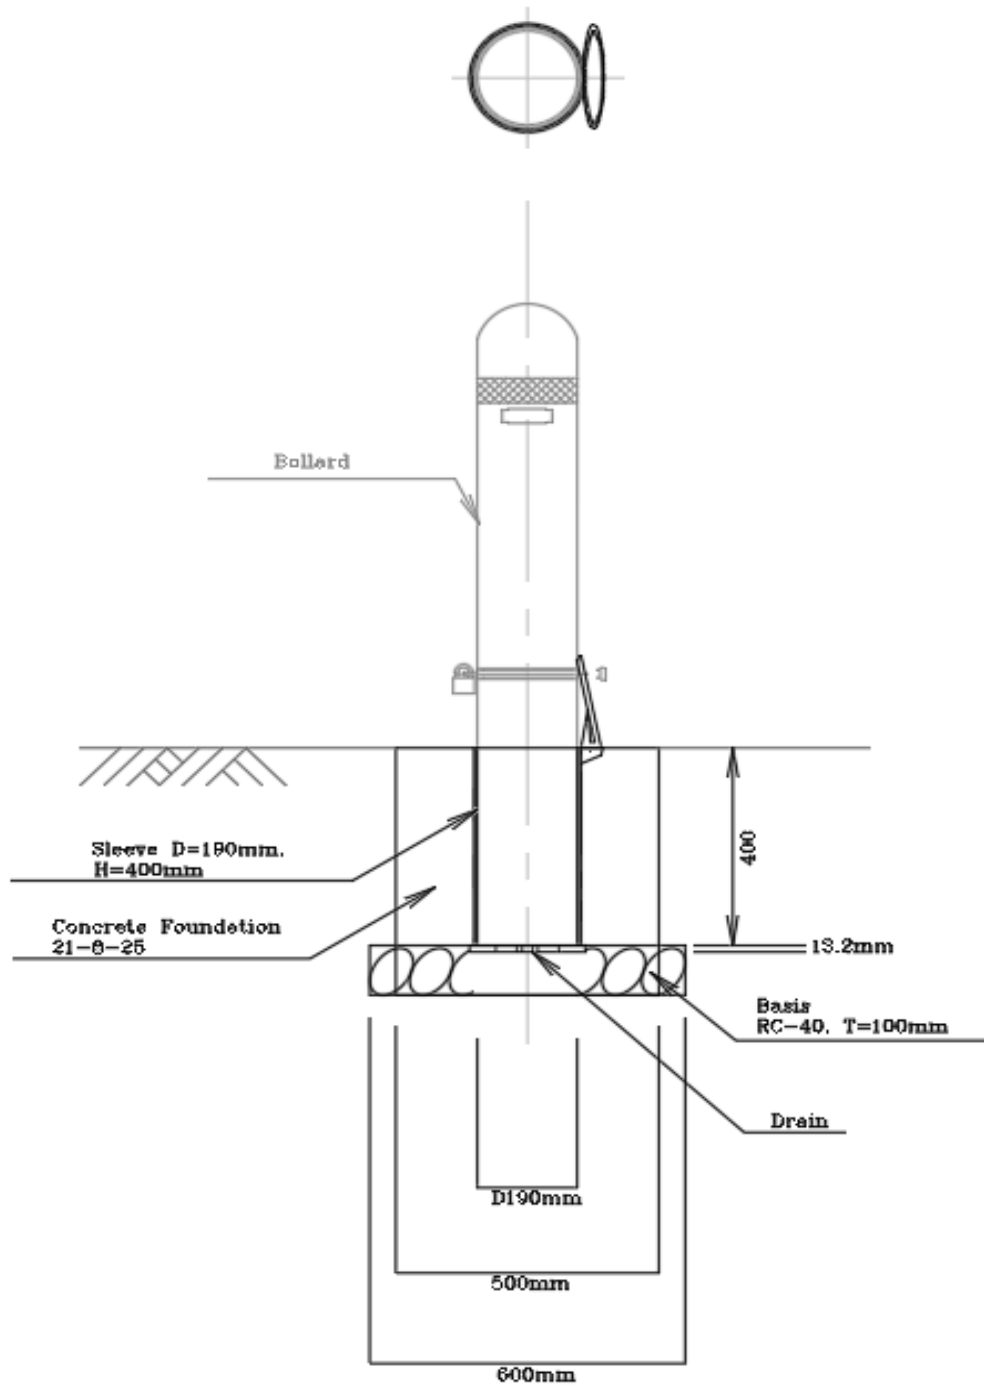

Unit: mm

BOLLARD SLEEVE DETAIL

Revised 1 May 26

	PROJECT TITLE:	RF.NO.	SHEET NUMBER			SEQ.NO.
DRAWING BY: NH	ROADS/PAVEMENTS & MISC. CIVIL WORK IDIQ CONTRACT		CLASS	LOG	SHEET	
CHECKED BY: NH	BOLLARD SLEEVE DETAIL	C-11r			17 OF 18	17



AF DÉCOR and all characters shall be white space on dark browned background.

Unit: mm

CONSTRUCTION SIGN

	PROJECT TITLE:	RF.NO.	SHEET NUMBER			SEQ.NO.
DRAWING BY: NH	ROADS/PAVEMENTS & MISC. CIVIL WORK IDIQ CONTRACT		CLASS	LOG	SHEET	
CHECKED BY: NH	CONSTRUCTION SIGN	C-12			18 OF 18	18