

Attachment 1

Facility Plans

FLOOR PLAN

Fort Campbell
Building 95

Keyed Notes:

- 1. Existing Rectifier and Inverter equipment to be removed.
- 2. New Rectifier and Inverter equipment to be installed.

Legend

Existing Cable Ladder

New Cable Ladder

Existing Equipment Being Used


Existing

New Install

Decommissioning

Cabling Legend

- Power
- 4-6 Strand
- Fiber
- RJ21
- Copper
- Grounding

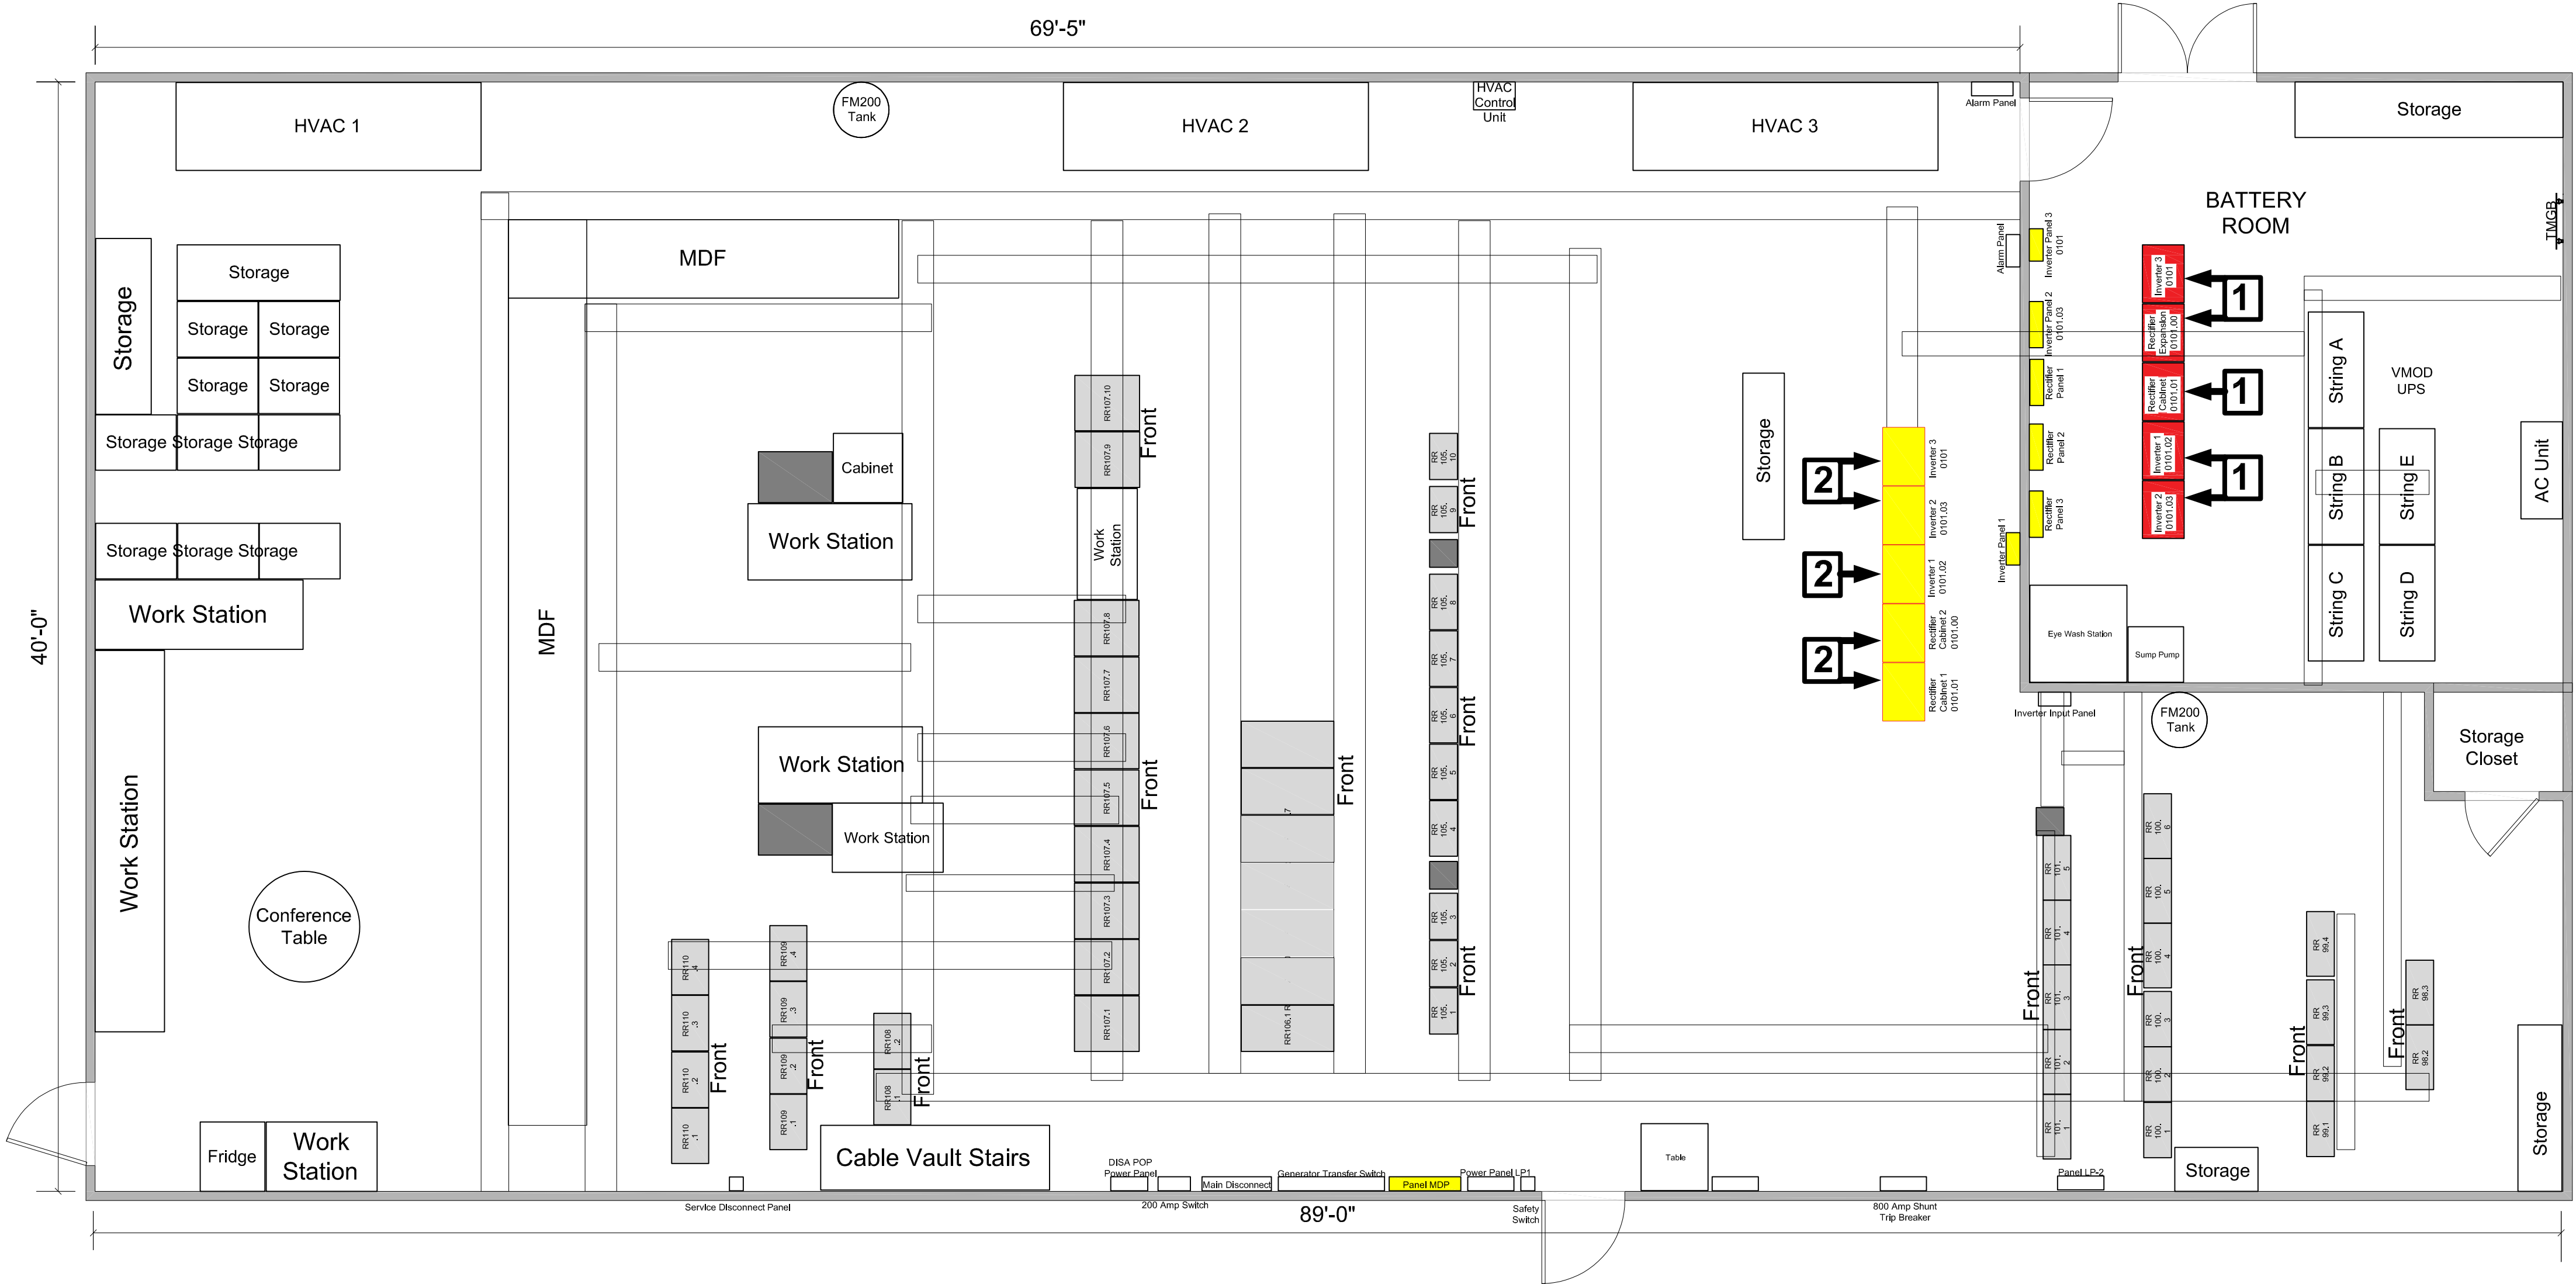

REVISION HISTORY				
REV	DESCRIPTION	DATE	WORK ID	BY


Installation Information Infrastructure Modernization Program (I3MP)				
PROJECT NAME: RECTIFIER/INVERTER REPLACEMENT RFP				
SHEET 1 OF 7		SCALE: 1/4" = 1'		
FILENAME: FTC RR_BLDG 95.DWG				
SHEET TITLE: Floor Plan				
SITE: Fort Campbell		Bldg: Bldg 95		Room:

FLOOR PLAN

Keyed Notes:

- 1. Existing Rectifier and Inverter equipment to be removed.
- 2. New Rectifier and Inverter equipment to be installed.

Fort Campbell
Building 2579

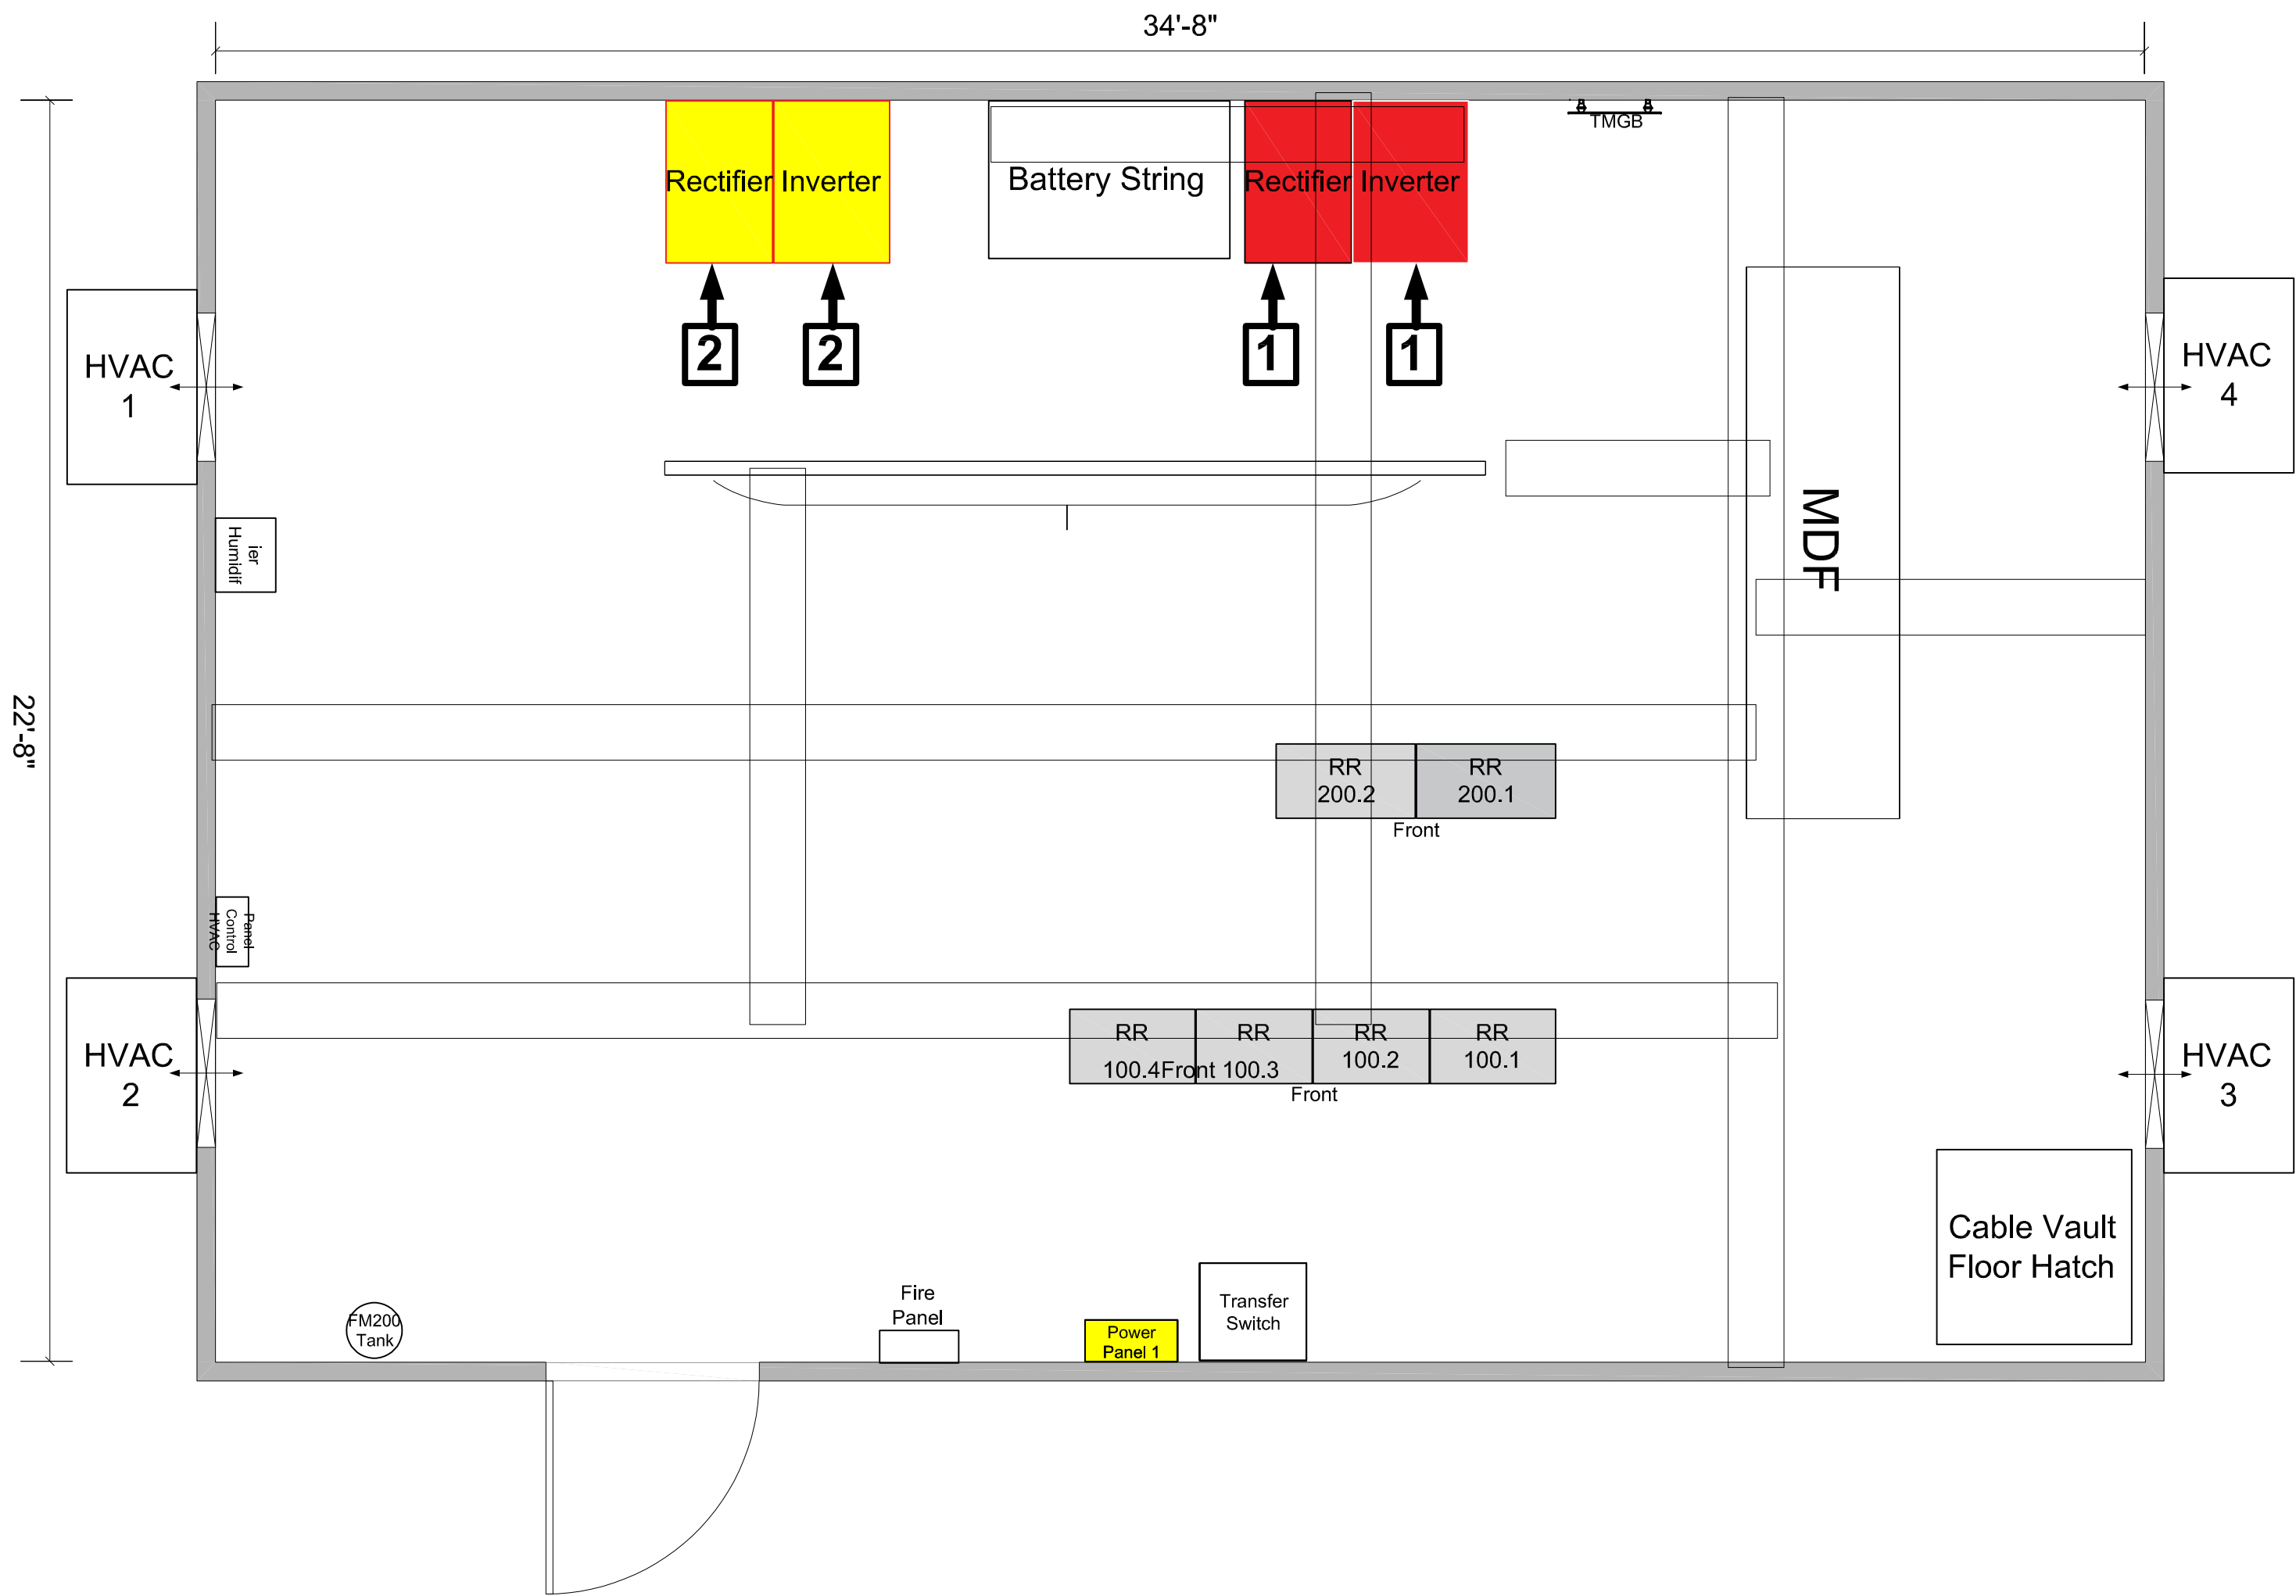

Legend

Existing Cable Ladder

New Cable Ladder

Existing Equipment Being Used

New Install

Existing

Decommissioning

Cabling Legend

- Power
- 48-600V
- Fiber
- RJ45
- Copper
- Grounding

REVISION HISTORY				
REV	DESCRIPTION	DATE	WORK ID	BY

Installation Information Infrastructure Modernization Program (I3MP)			
PROJECT NAME: RECTIFIER/INVERTER REPLACEMENT RFP			
SHEET 2	OF 7	SCALE: 3/8" = 1'	SIZE: D
FILENAME: FTC_RR_BLDG_2579			
SHEET TITLE: Floor Plan			
SITE:	Fort Campbell	Bldg:	Bldg 2579
		Room:	

FLOOR PLAN

Keyed Notes:

- 1. Existing Rectifier and Inverter equipment to be removed.
- 2. New Rectifier and Inverter equipment to be installed.
- 3. Relocated Eye Wash Station to accommodate new Rectifier and Inverter equipment.

Fort Campbell
Building 6079

Legend

Existing Cable Ladder

New Cable Ladder

Existing Equipment Being Used

Existing

Decommissioning

New Install

Cabling Legend

Power


48-600V AC

Fiber

RJ45

Copper

Grounding

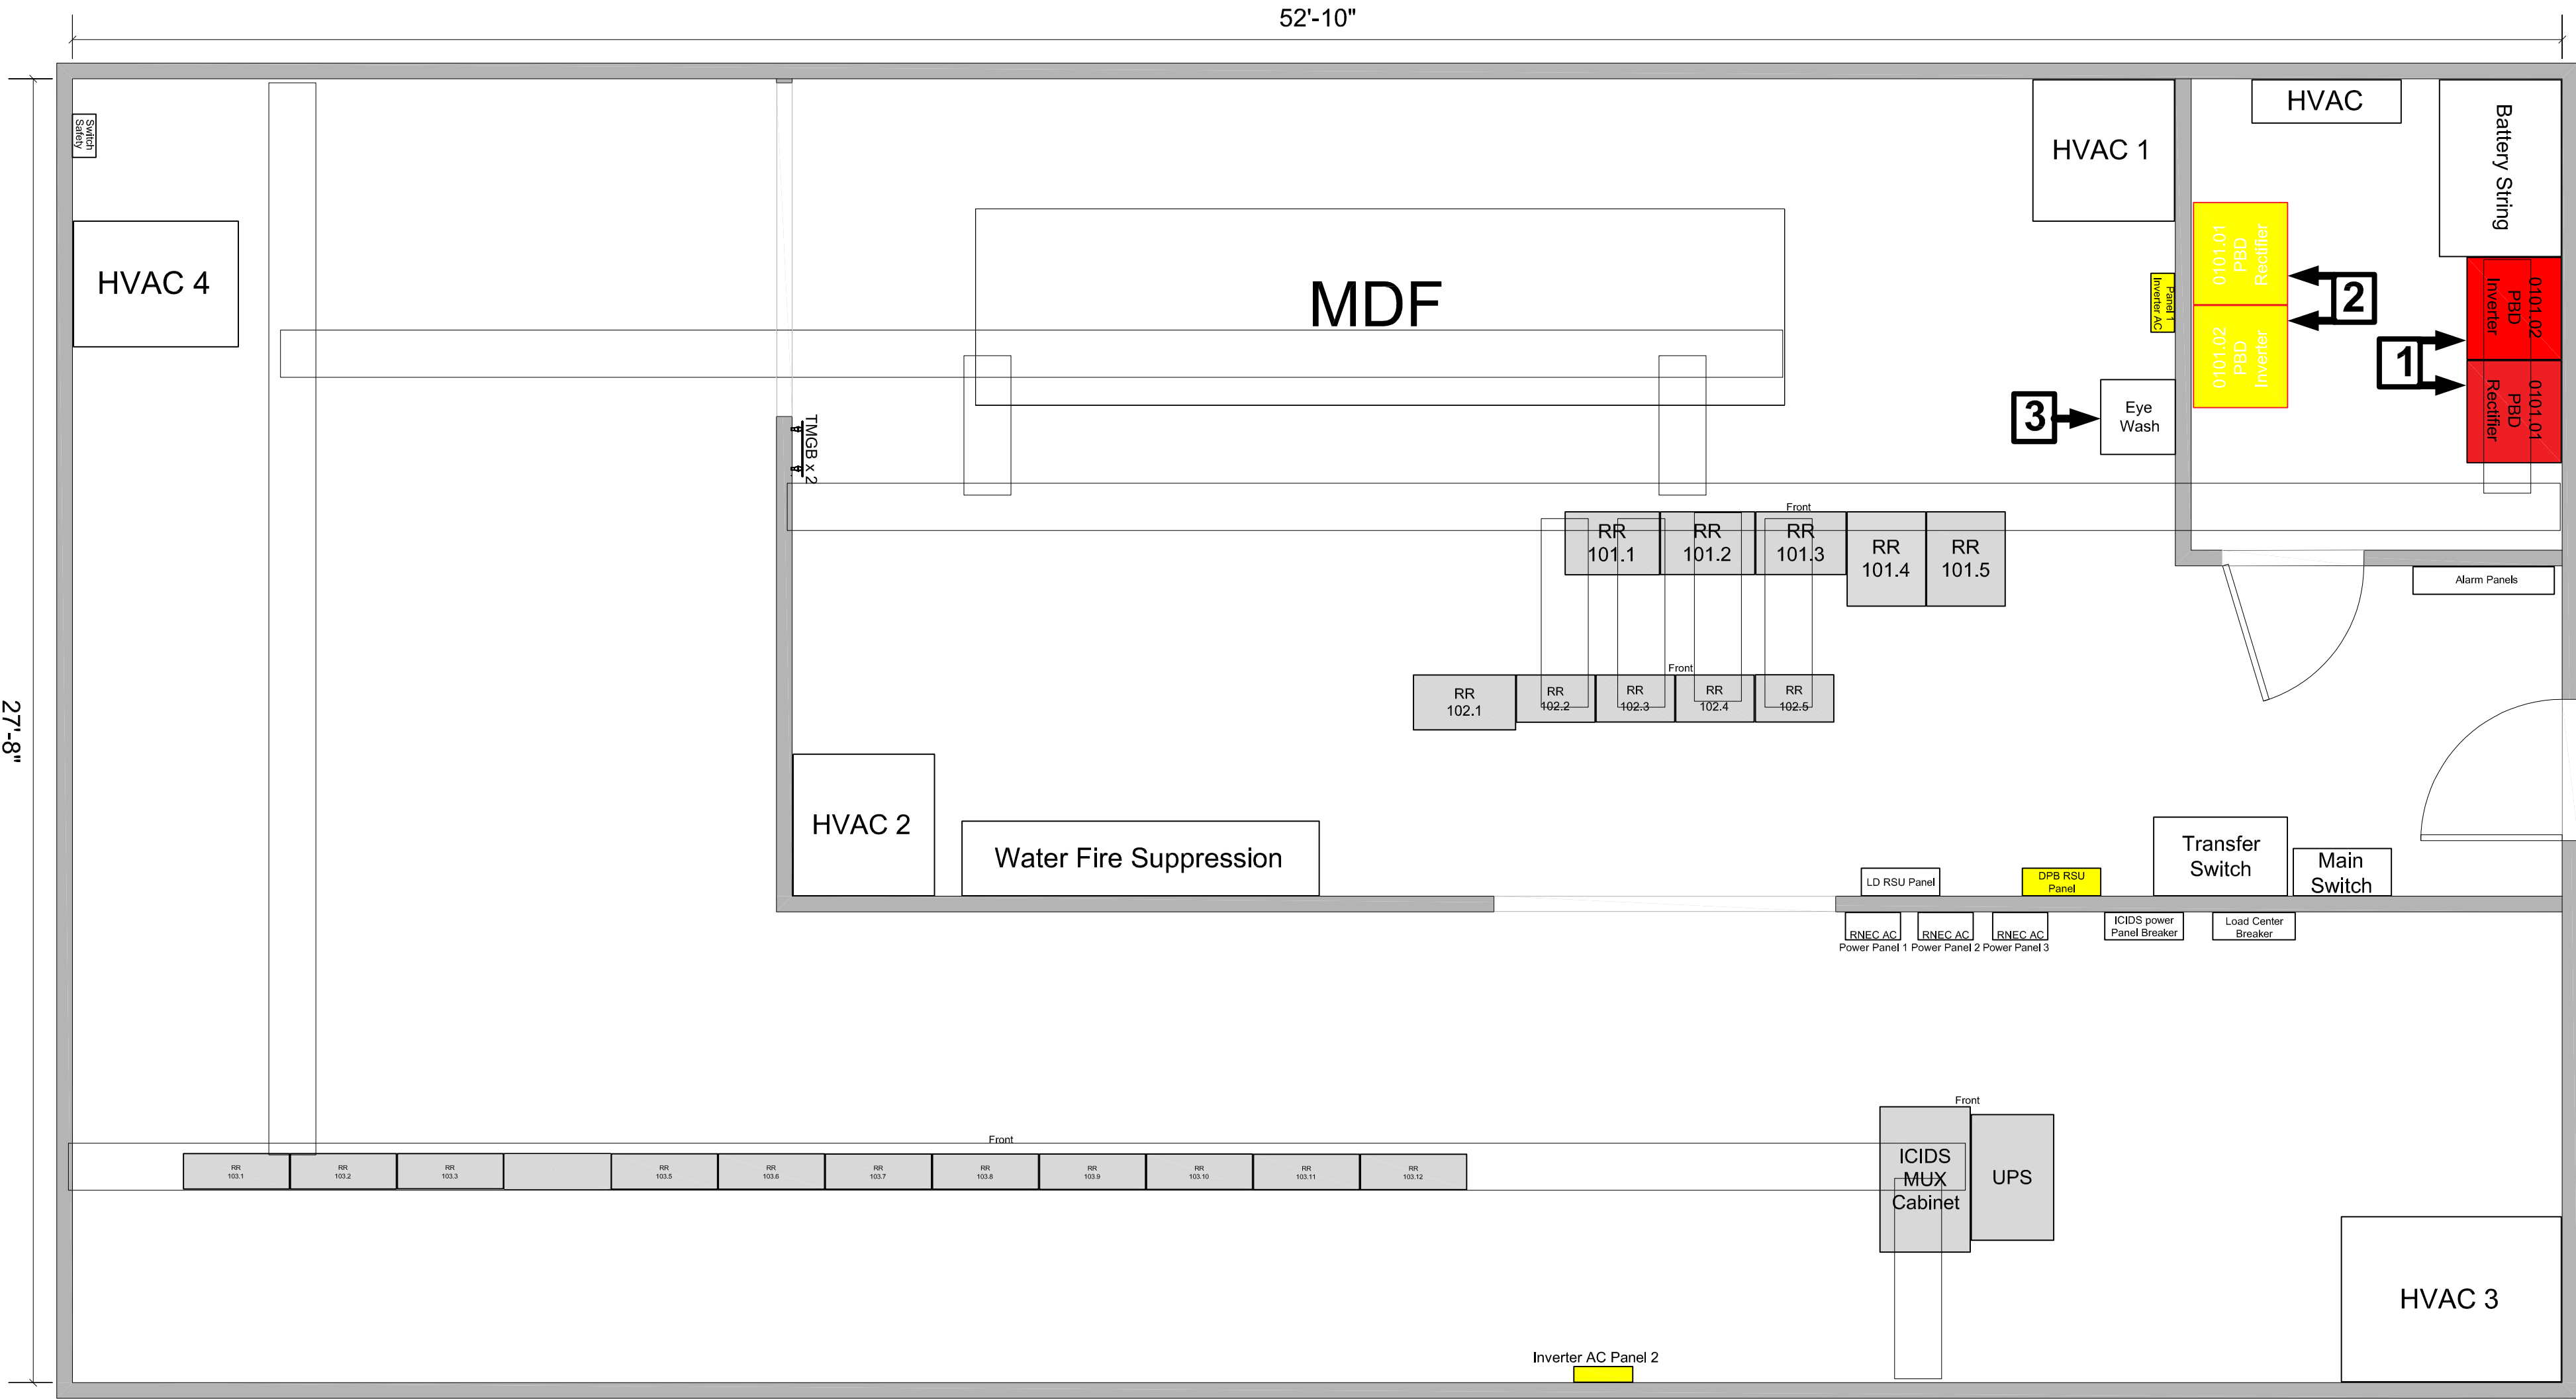

REVISION HISTORY				
REV	DESCRIPTION	DATE	WORK ID	BY

Installation Information Infrastructure Modernization Program (I3MP)				
PROJECT NAME: US ARMY VOICE MODERNIZATION				
SHEET 3	OF 7	SCALE: 3/8" = 1'	SIZE: D	
FILENAME: FTC RR_BLDG_6079.DWG				
SHEET TITLE: Floor Plan				
SITE:	Fort Campbell	Bldg:	Bldg 6079	Room:

FLOOR PLAN

Keyed Notes:

- 1. Existing Rectifier and Inverter equipment to be removed.
- 2. New Rectifier and Inverter equipment to be installed.
- 3. Existing rack relocated/removed to accommodate new equipment. Empty power rack currently where new Rectifier cabinet is being located.

Fort Campbell
Building 6642

Legend

Existing Cable Ladder

New Cable Ladder

Existing Equipment Being Used


Existing

Decommissioning

New Install

Cabling Legend

- Power
- AC Ground
- Fiber
- RJ45
- Copper
- Grounding

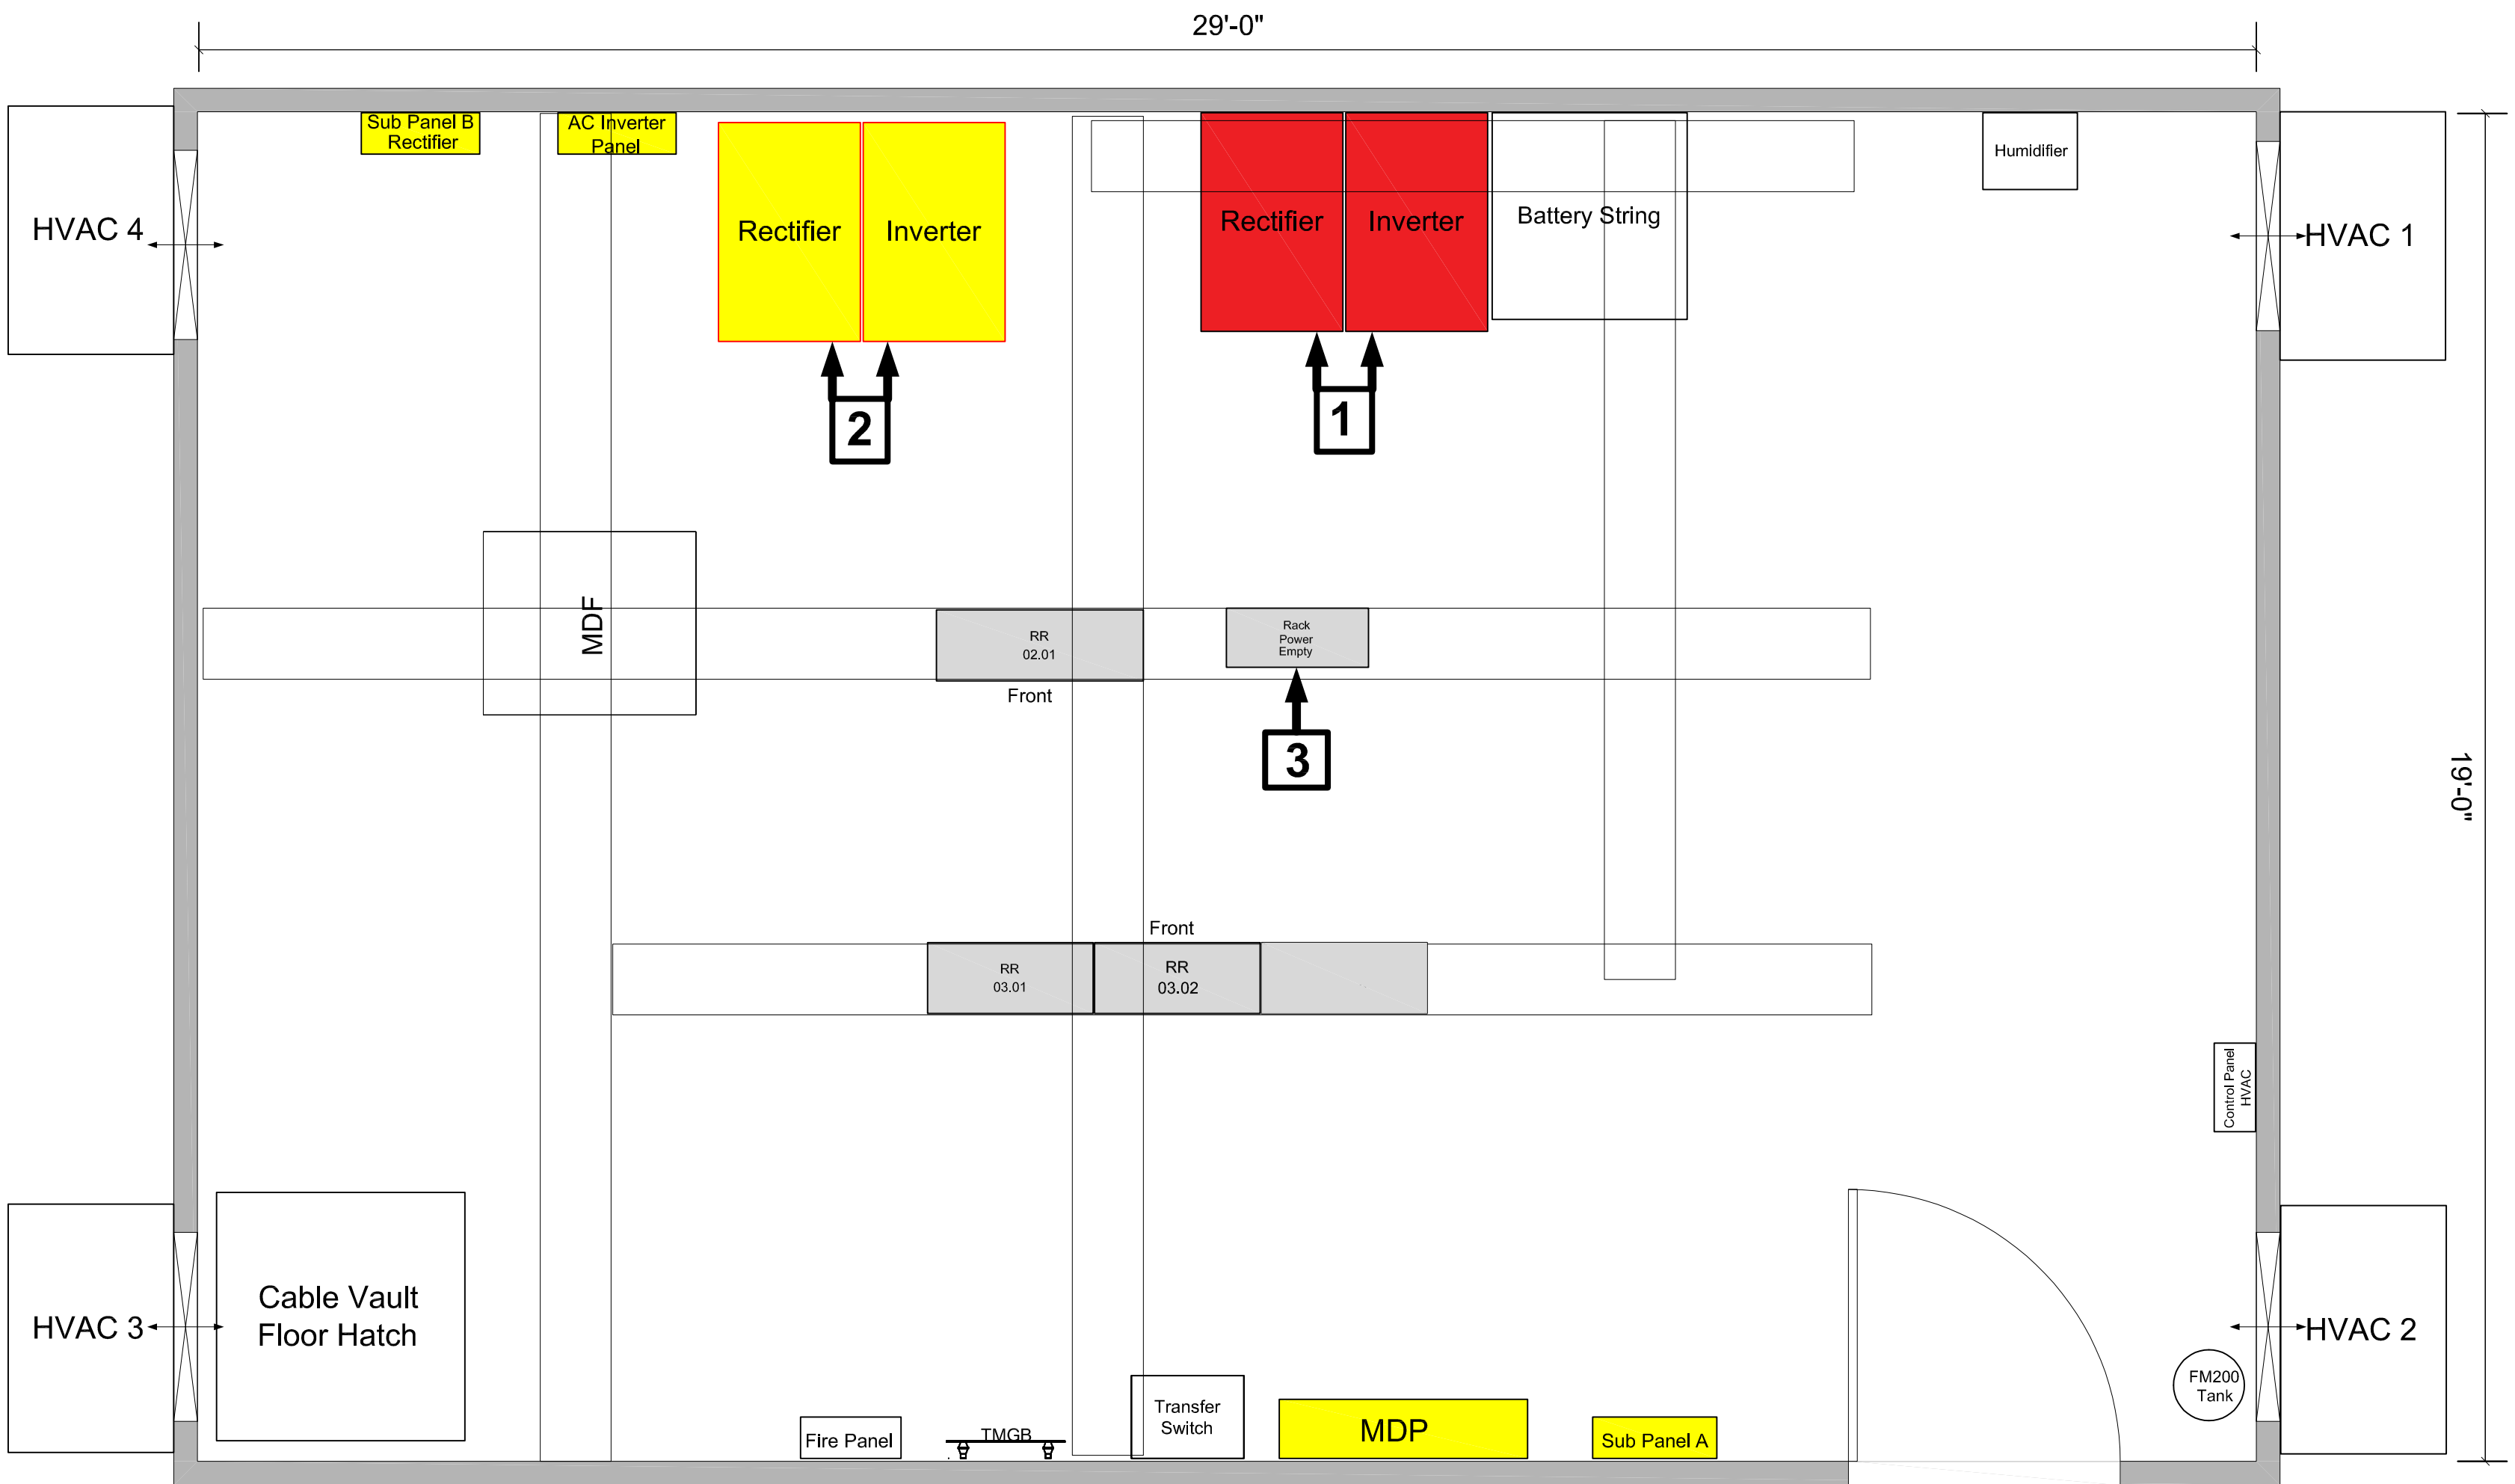

REVISION HISTORY				
REV	DESCRIPTION	DATE	WORK ID	BY

Installation Information Infrastructure Modernization Program (I3MP)			
PROJECT NAME: RECTIFIER/INVERTER REPLACEMENT RFP			
SHEET 4	OF 7	SCALE: 1/2" = 1'	SIZE: D
FILENAME: FTC RR_BLDG_6642.DWG			
SHEET TITLE: Floor Plan			
SITE: Fort Campbell	Bldg: Bldg 6642	Room:	

FLOOR PLAN

Fort Campbell
Building 7030

Keyed Notes:

- 1. Existing Rectifier and Inverter equipment to be removed.
- 2. New Rectifier and Inverter equipment to be installed.

Existing Cable Ladder

New Cable Ladder

Existing Equipment Being Used

Existing

New Install

Decommissioning

Cabling Legend

Power


Grounding

Fiber

RJ45

Copper

Grounding

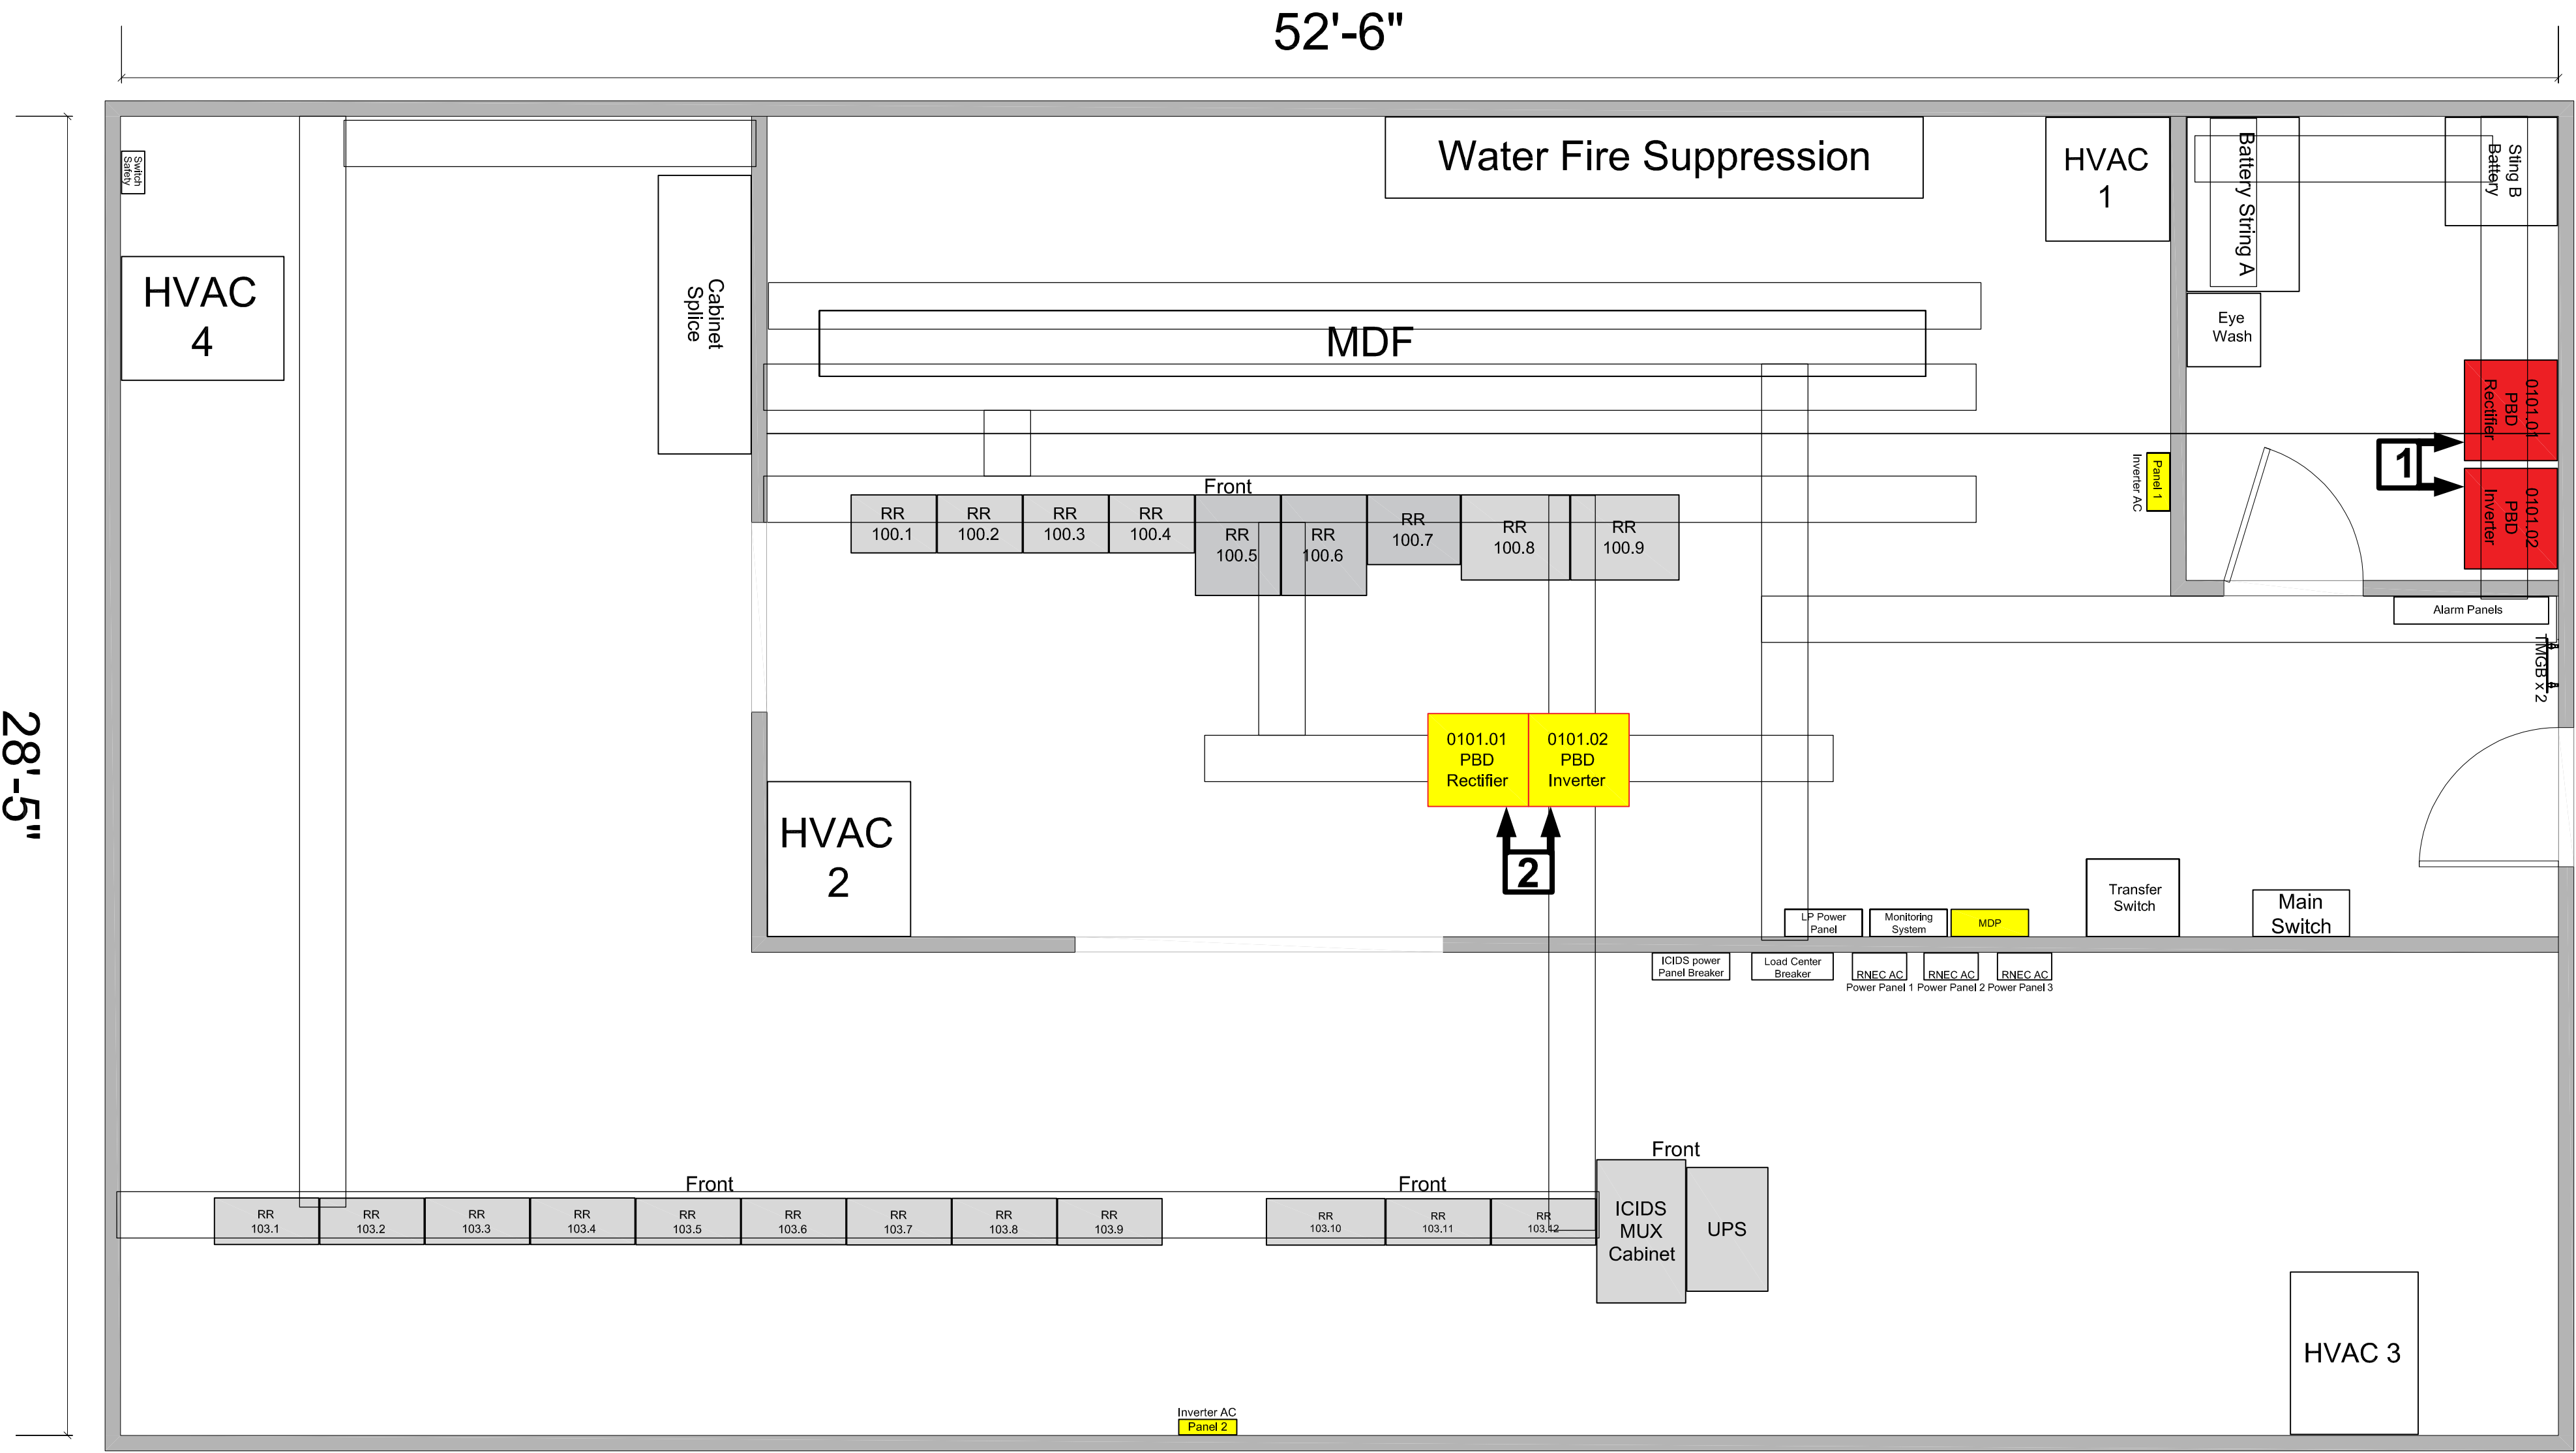

REVISION HISTORY				
REV	DESCRIPTION	DATE	WORK ID	BY


Installation Information Infrastructure Modernization Program (I3MP)			
PROJECT NAME: RECTIFIER/INVERTER REPLACEMENT RFP			
SHEET 5	OF 7	SCALE: 3/8" = 1'	SIZE: D
FILENAME: FTC_RR_BLDG_7030.DWG			
SHEET TITLE: Floor Plan			
SITE: Fort Campbell	Bldg: Bldg 7030	Room:	

FLOOR PLAN

Keyed Notes:

- 1. Existing Rectifier and Inverter equipment to be removed.
- 2. New Rectifier and Inverter equipment to be installed.
- 3. Existing equipment that can be removed/relocated to accommodate new equipment.

Fort Campbell
Building 7943

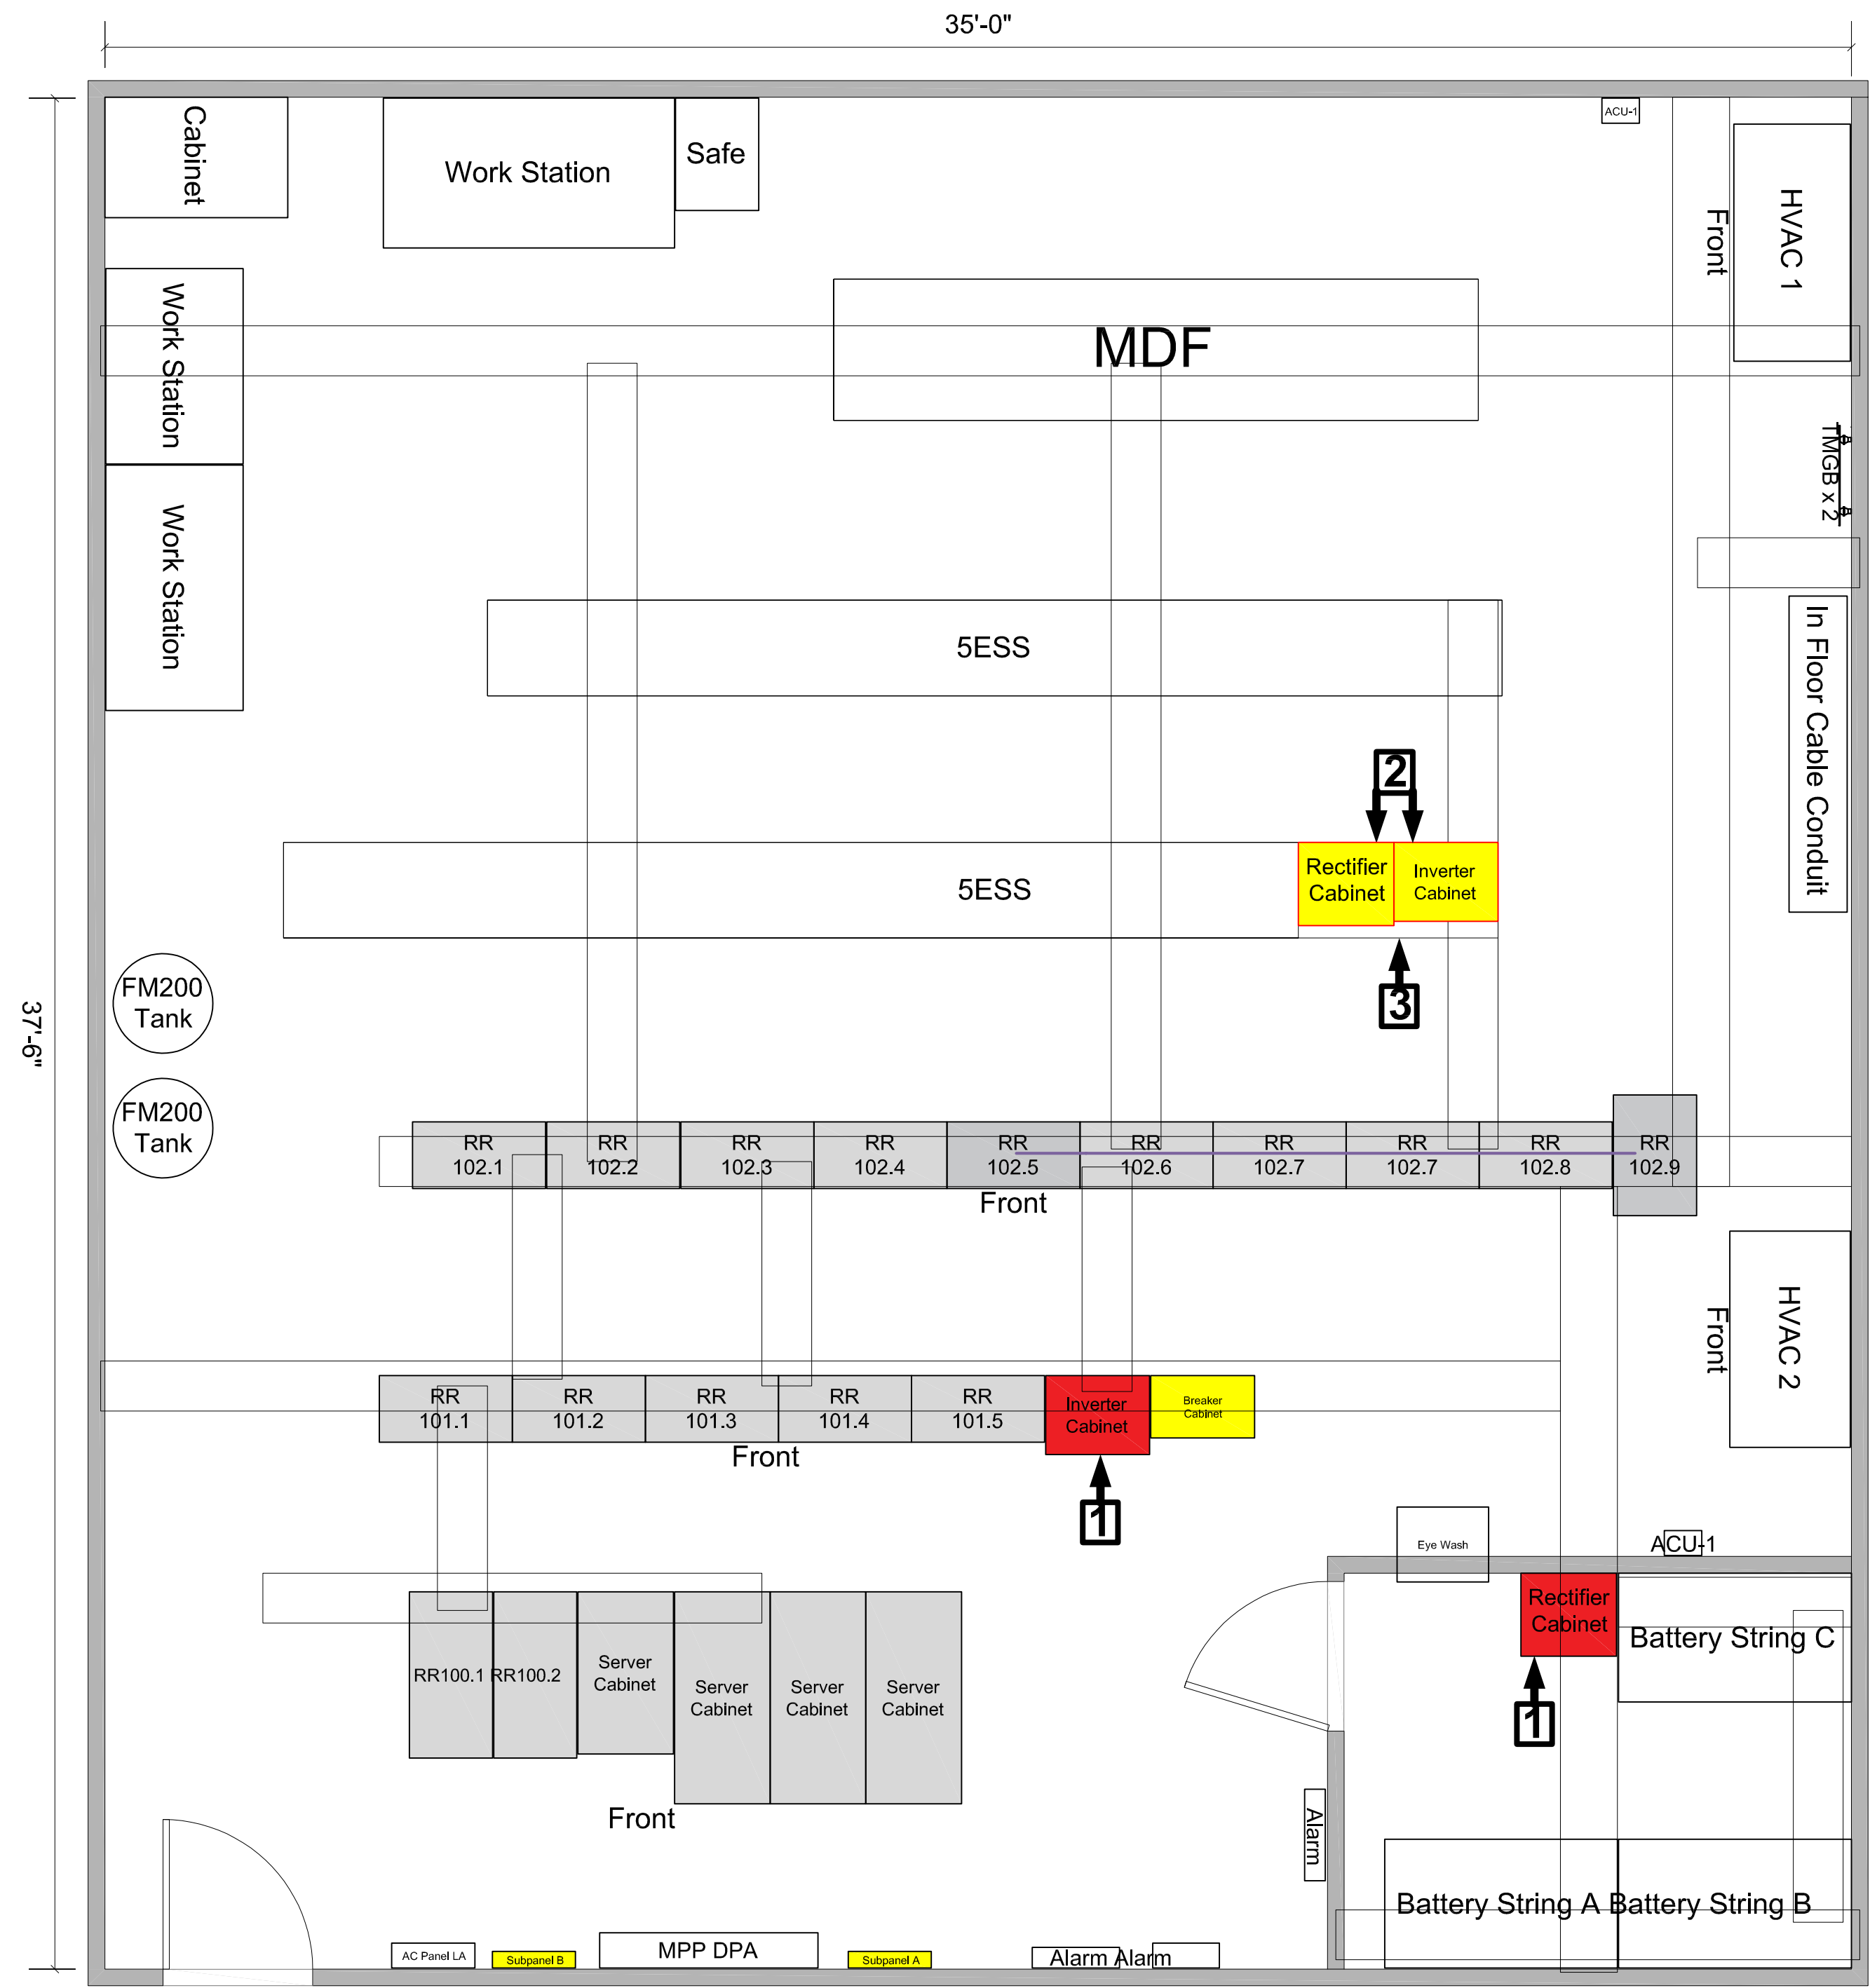

Legend

Existing Cable Ladder

New Cable Ladder

Existing Equipment Being Used

Existing

New Install

Decommissioning

Cabling Legend

- Power
- Video
- Fiber
- RJ45
- Copper
- Grounding

UNCLASSIFIED

REVISION HISTORY				
REV	DESCRIPTION	DATE	WORK ID	BY

Installation Information Infrastructure Modernization Program (I3MP)			
PROJECT NAME: RECTIFIER/INVERTER REPLACEMENT RFP			
SHEET 6	OF 7	SCALE: 3/8" = 1'	SIZE: D
FILENAME: FTC_RR_BLDG_7943.DWG			
SHEET TITLE: Floor Plan			
SITE: Fort Campbell	Bldg: Bldg 7943	Room:	

CONCEPT SUBMITTAL

FLOOR PLAN

Keyed Notes:

- 1. Existing Rectifier and Inverter equipment to be removed.
- 2. New Rectifier and Inverter equipment to be installed.
- 3. Existing rack relocated/removed to accommodate new equipment. Empty power rack currently where new Rectifier cabinet is being located.

Fort Campbell
Building B7254

Legend

Existing Cable Ladder

New Cable Ladder

Existing Equipment Being Used


New Install

Existing

Decommissioning

Cabling Legend

- Power
- AC Grounding
- Fiber
- RJ45
- Copper
- Grounding

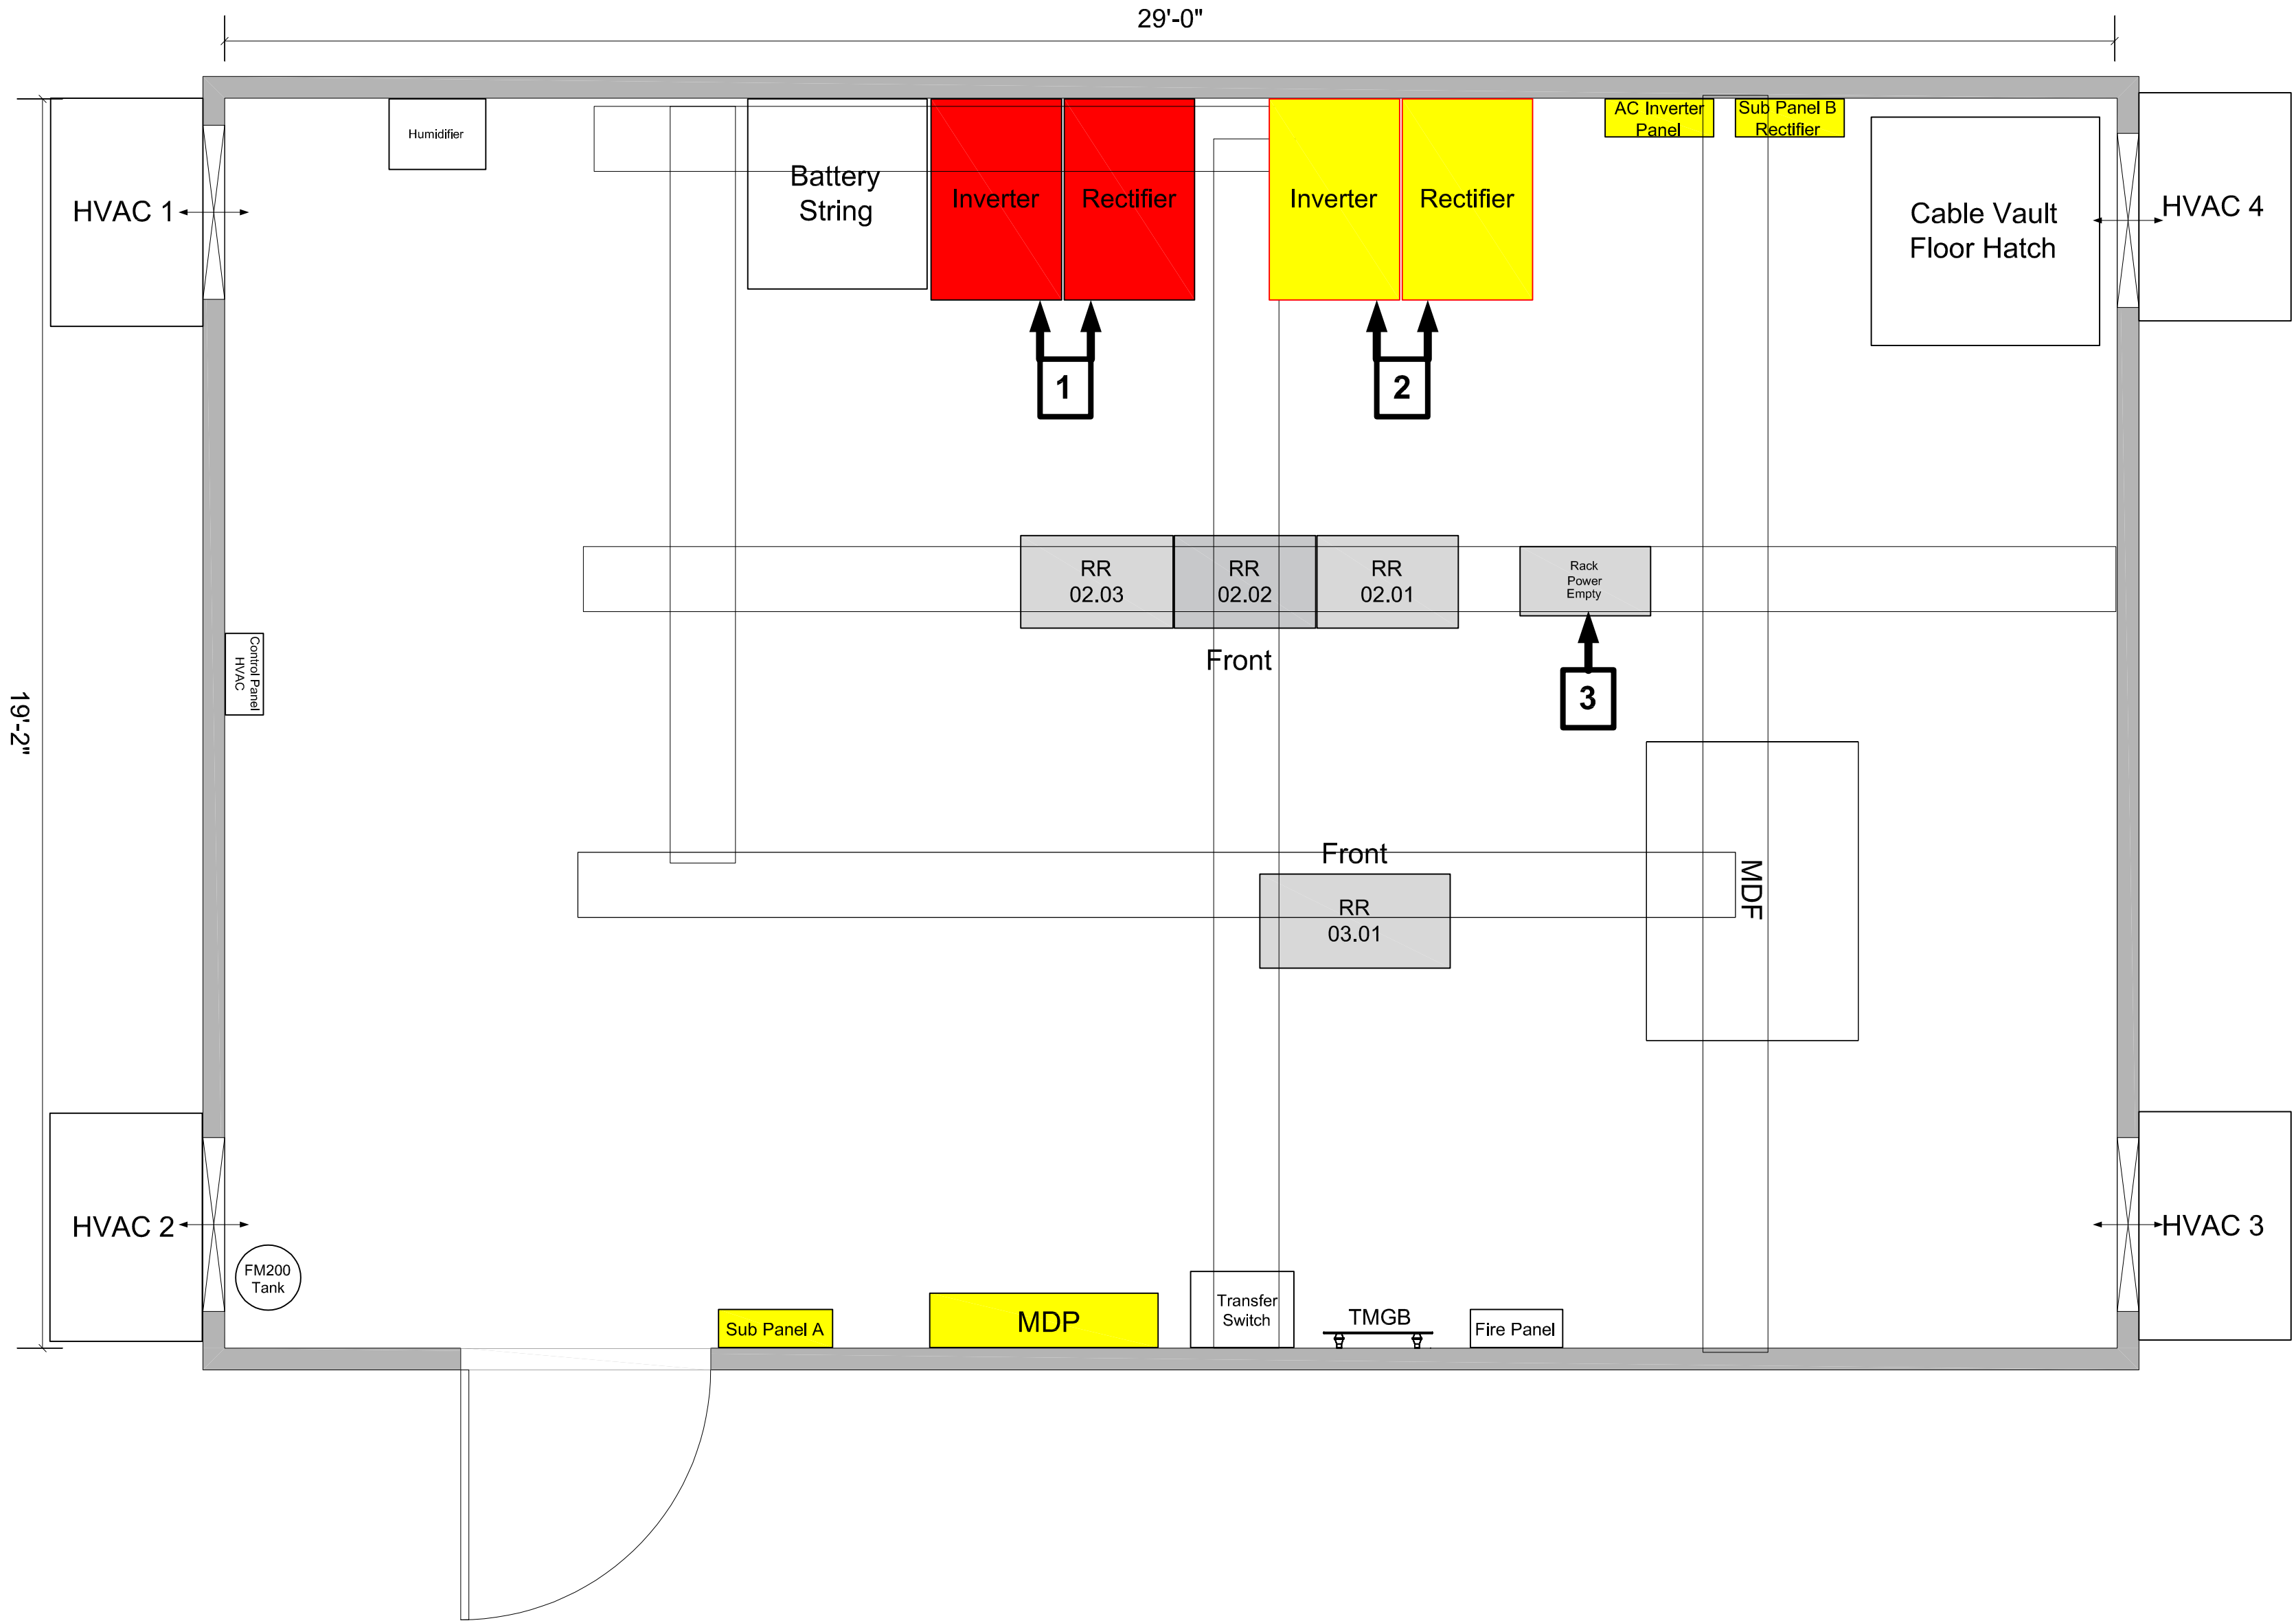

REVISION HISTORY				
REV	DESCRIPTION	DATE	WORK ID	BY

Installation Information Infrastructure Modernization Program (I3MP)		
PROJECT NAME: RECTIFIER/INVERTER REPLACEMENT RFP		
SHEET 7 OF 7	SCALE: NTS	
FILENAME: FTC_RR_BLDG_B7254.DWG		
SHEET TITLE: Floor Plan		
SITE: Fort Campbell	Bldg: Bldg B7254	Room: