


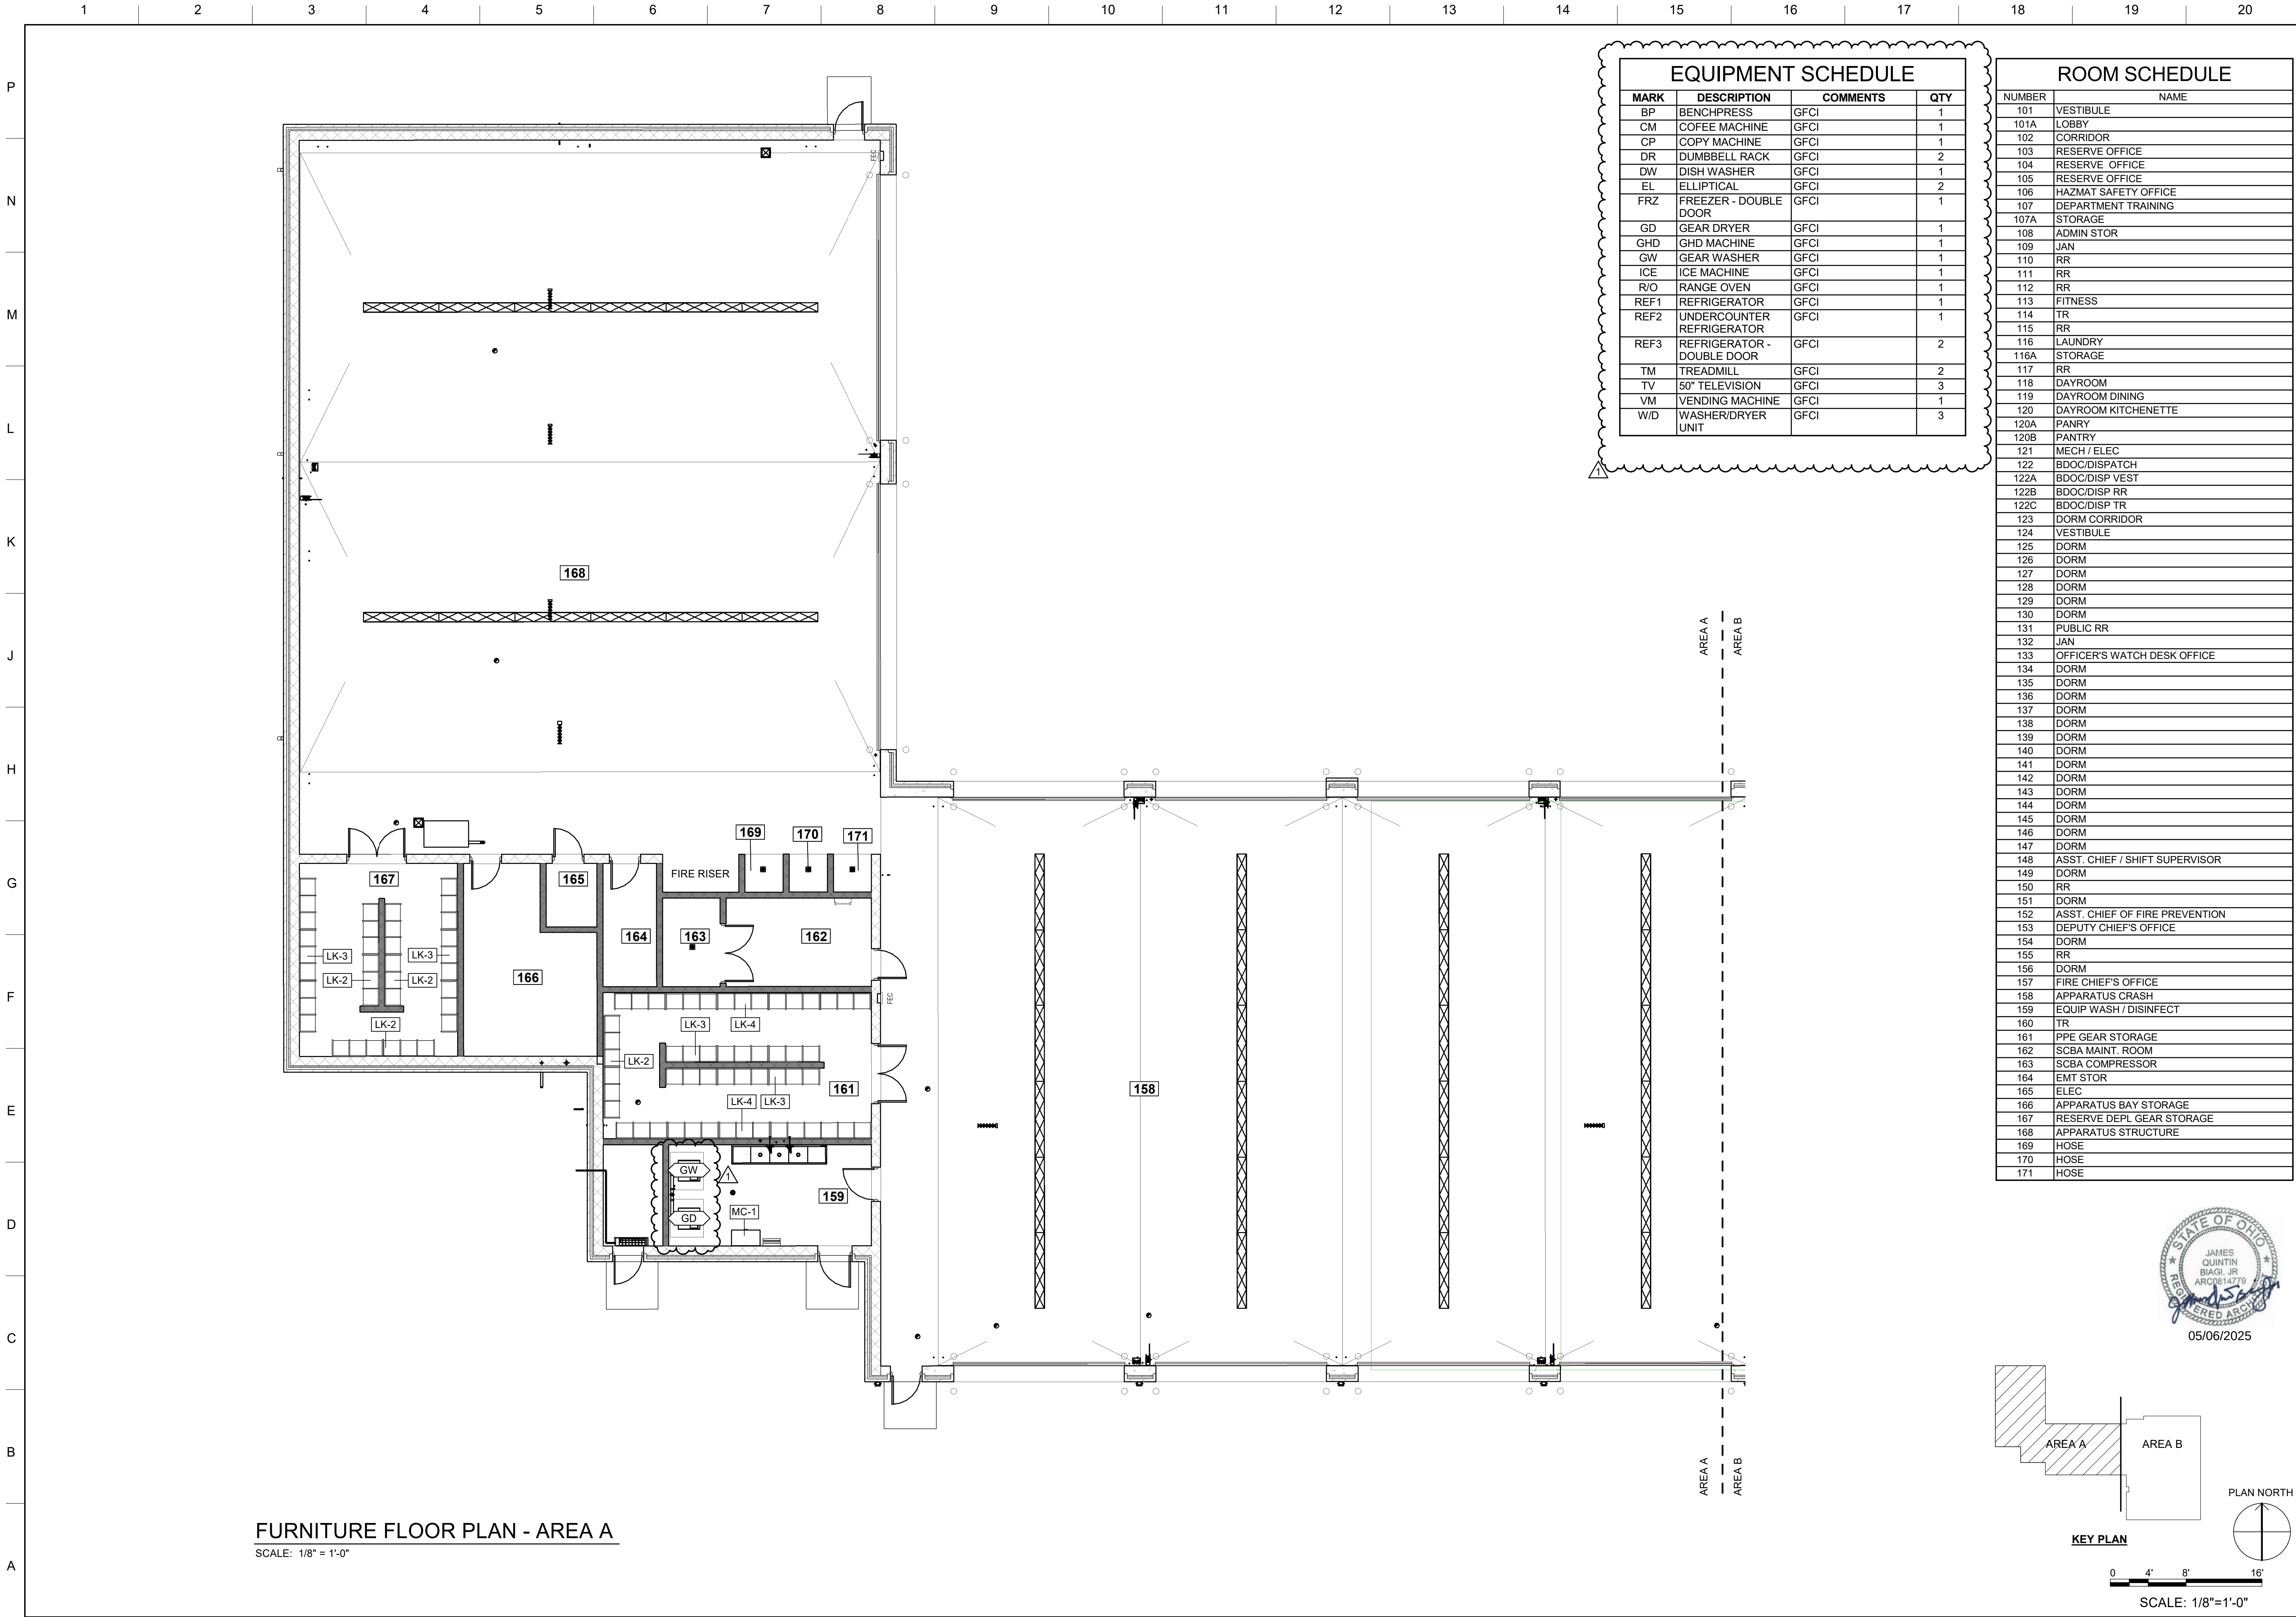



FURNITURE FLOOR PLAN - AREA A

SCALE: 1/8" = 1'-0"

EQUIPMENT SCHEDULE			
MARK	DESCRIPTION	COMMENTS	QTY
BP	BENCHPRESS	GFCI	1
CM	COFEE MACHINE	GFCI	1
CP	COPY MACHINE	GFCI	1
DR	DUMBBELL RACK	GFCI	2
DW	DISH WASHER	GFCI	1
EL	ELLIPTICAL	GFCI	2
FRZ	FREEZER - DOUBLE DOOR	GFCI	1
GD	GEAR DRYER	GFCI	1
GHD	GHD MACHINE	GFCI	1
GW	GEAR WASHER	GFCI	1
ICE	ICE MACHINE	GFCI	1
R/O	RANGE OVEN	GFCI	1
REF1	REFRIGERATOR	GFCI	1
REF2	UNDERCOUNTER REFRIGERATOR	GFCI	1
REF3	REFRIGERATOR - DOUBLE DOOR	GFCI	2
TM	TREADMILL	GFCI	2
TV	50" TELEVISION	GFCI	3
VM	VENDING MACHINE	GFCI	1
W/D	WASHER/DRYER UNIT	GFCI	3

ROOM SCHEDULE	
NUMBER	NAME
101	VESTIBULE
101A	LOBBY
102	CORRIDOR
103	RESERVE OFFICE
104	RESERVE OFFICE
105	RESERVE OFFICE
106	HAZMAT SAFETY OFFICE
107	DEPARTMENT TRAINING
107A	STORAGE
108	ADMIN STOR
109	JAN
110	RR
111	RR
112	RR
113	FITNESS
114	TR
115	RR
116	LAUNDRY
116A	STORAGE
117	RR
118	DAYROOM
119	DAYROOM DINING
120	DAYROOM KITCHENETTE
120A	PANTRY
120B	PANTRY
121	MECH / ELEC
122	BDOC/DISPATCH
122A	BDOC/DISP VEST
122B	BDOC/DISP RR
122C	BDOC/DISP TR
123	DORM CORRIDOR
124	VESTIBULE
125	DORM
126	DORM
127	DORM
128	DORM
129	DORM
130	DORM
131	PUBLIC RR
132	JAN
133	OFFICER'S WATCH DESK OFFICE
134	DORM
135	DORM
136	DORM
137	DORM
138	DORM
139	DORM
140	DORM
141	DORM
142	DORM
143	DORM
144	DORM
145	DORM
146	DORM
147	DORM
148	ASST. CHIEF / SHIFT SUPERVISOR
149	DORM
150	RR
151	DORM
152	ASST. CHIEF OF FIRE PREVENTION
153	DEPUTY CHIEF'S OFFICE
154	DORM
155	RR
156	DORM
157	FIRE CHIEF'S OFFICE
158	APPARATUS CRASH
159	EQUIP WASH / DISINFECT
160	TR
161	PPE GEAR STORAGE
162	SCBA MAINT. ROOM
163	SCBA COMPRESSOR
164	EMT STOR
165	ELEC
166	APPARATUS BAY STORAGE
167	RESERVE DEPL GEAR STORAGE
168	APPARATUS STRUCTURE
169	HOSE
170	HOSE
171	HOSE

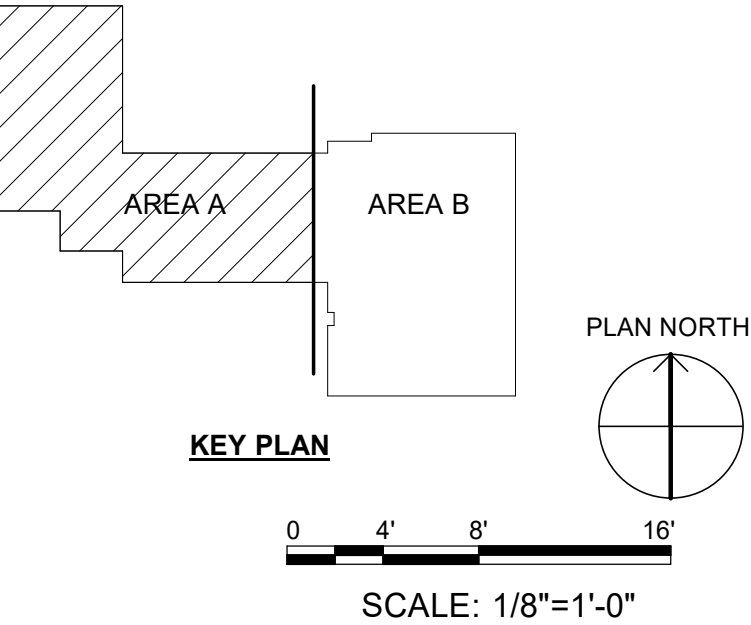

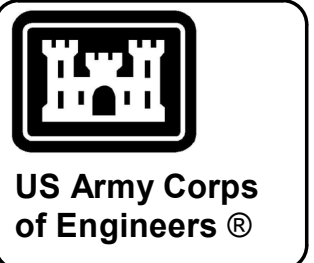

US Army Corps of Engineers®

ISSUE DATE:
26 NOVEMBER 2024

DESIGNED BY:
T. HOUGHAN

LOUISVILLE DISTRICT
LOUISVILLE, KY 40202

SOLICITATION NO.:

CHECKED BY:
M. ARMISTEAD

CONTRACT NO.:

SUBMITTED BY:
M. BERNINGER

AMENDMENT 0004

1

MARK

05/06/25

DATE

US ARMY CORPS OF ENGINEERS
LOUISVILLE DISTRICT
600 DR. MARTIN LUTHER KING, JR. PLACE
LOUISVILLE, KY 40202




JOEL 239001 BASE FIRE STATION YOUNGSTOWN AIR RESERVE STATION, OH

P#: 513392



FURNITURE FLOOR PLAN AREA A

SHEET ID

I-105

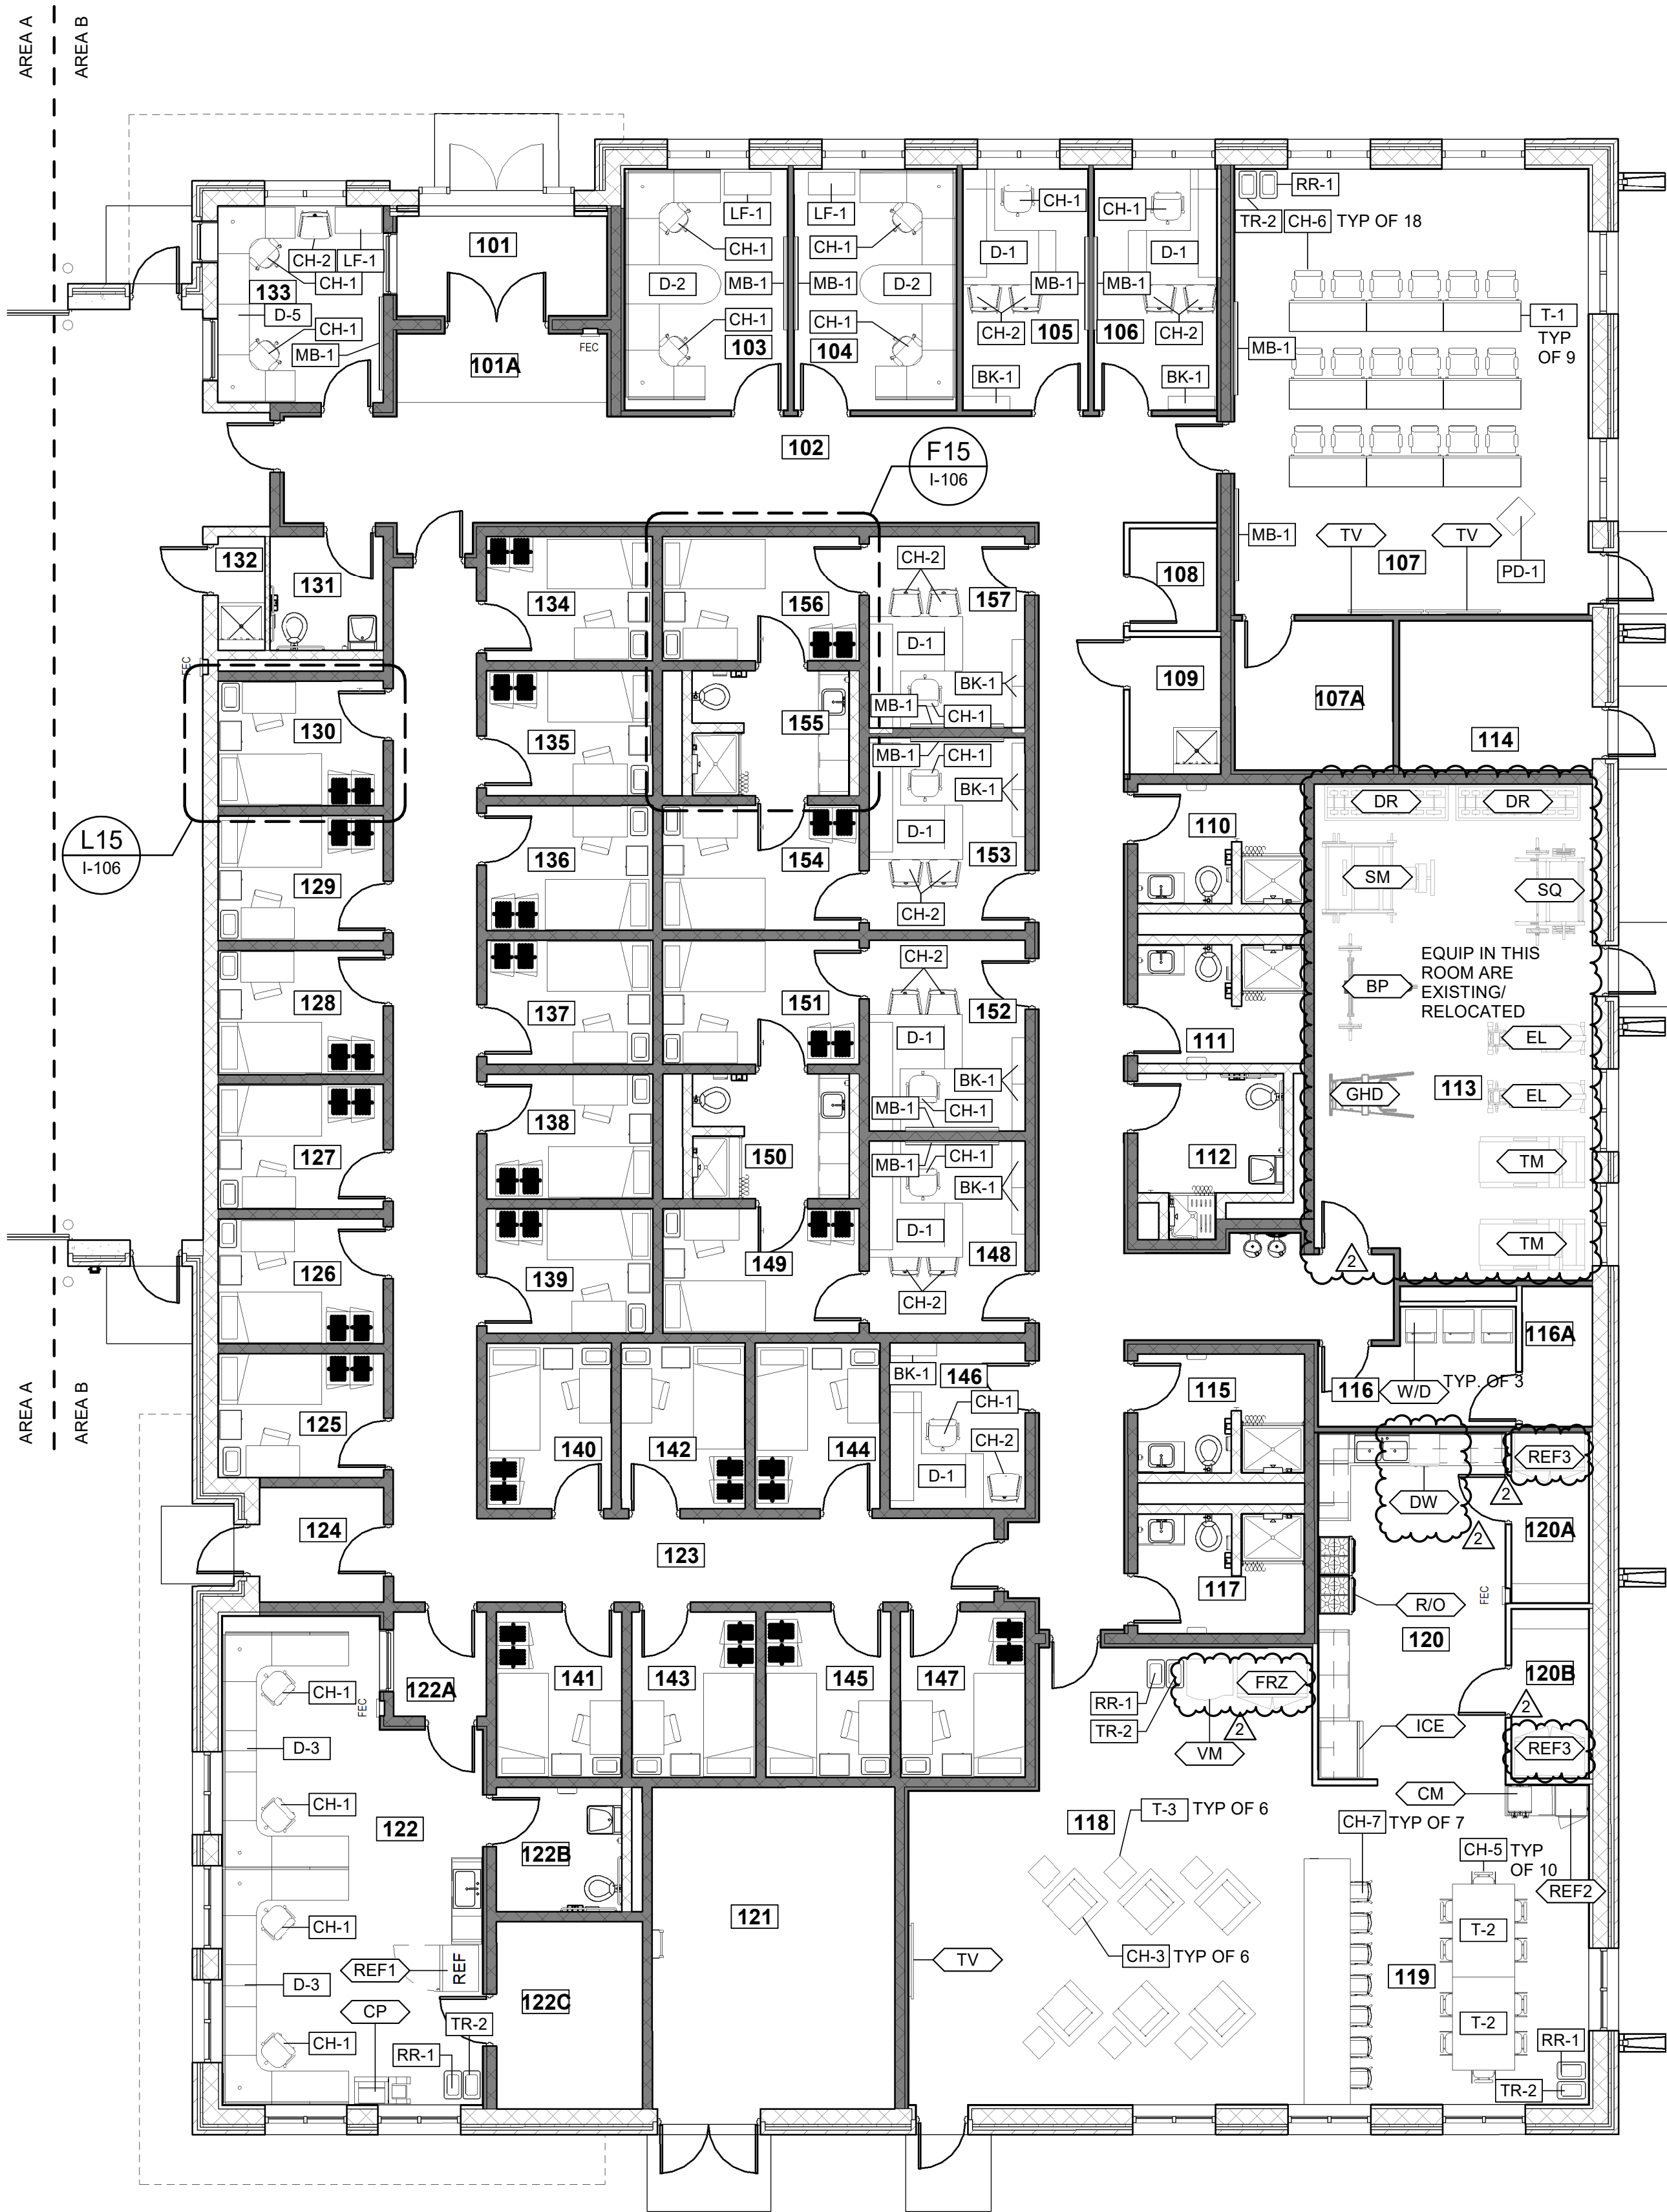


FURNITURE FLOOR PLAN - AREA B
SCALE: 1/8" = 1'-0"

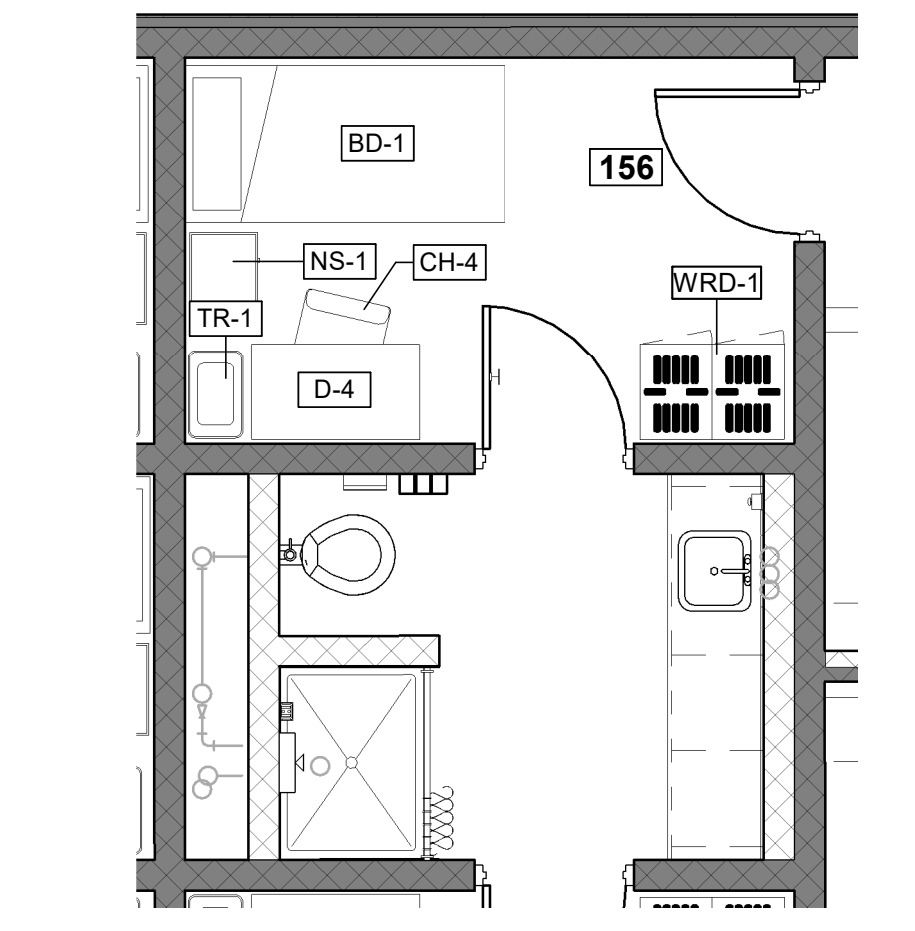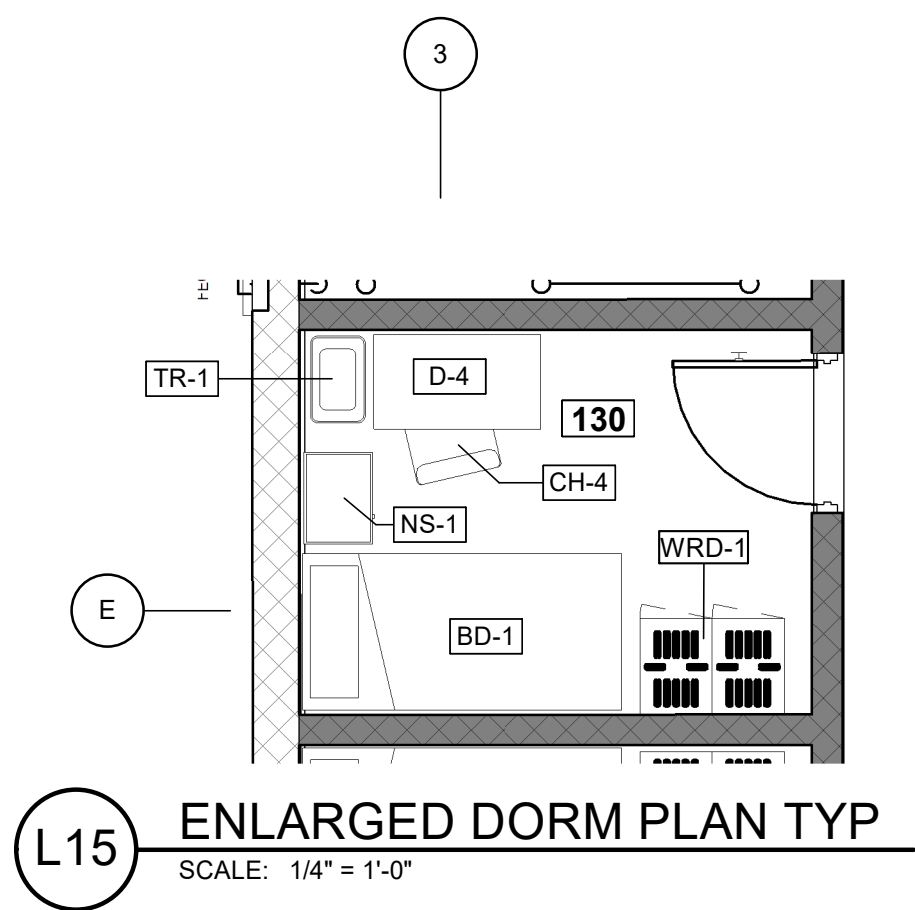




EQUIPMENT SCHEDULE			
MARK	DESCRIPTION	COMMENTS	QTY
BP	BENCHPRESS	GFCI	1
CM	COFEE MACHINE	GFCI	1
CP	COPY MACHINE	GFCI	1
DR	DUMBBELL RACK	GFCI	2
DW	DISH WASHER	GFCI	1
EL	ELLIPTICAL	GFCI	2
FRZ	FREEZER - DOUBLE DOOR	GFCI	1
GD	GEAR DRYER	GFCI	1
GHD	GHD MACHINE	GFCI	1
GW	GEAR WASHER	GFCI	1
ICE	ICE MACHINE	GFCI	1
R/O	RANGE OVEN	GFCI	1
REF1	REFRIGERATOR	GFCI	1
REF2	UNDERCOUNTER REFRIGERATOR	GFCI	1
REF3	REFRIGERATOR - DOUBLE DOOR	GFCI	2
TM	TREADMILL	GFCI	2
TV	50" TELEVISION	GFCI	3
VM	VENDING MACHINE	GFCI	1
W/D	WASHER/DRYER UNIT	GFCI	3

ROOM SCHEDULE	
NUMBER	NAME
101	VESTIBULE
101A	LOBBY
102	CORRIDOR
103	RESERVE OFFICE
104	RESERVE OFFICE
105	RESERVE OFFICE
106	HAZMAT SAFETY OFFICE
107	DEPARTMENT TRAINING
107A	STORAGE
108	ADMIN STOR
109	JAN
110	RR
111	RR
112	RR
113	FITNESS
114	TR
115	RR
116	LAUNDRY
116A	STORAGE
117	RR
118	DAYROOM
119	DAYROOM DINING
120	DAYROOM KITCHENETTE
120A	PANTRY
120B	PANTRY
121	MECH / ELEC
122	BDOC/DISPATCH
122A	BDOC/DISP VEST
122B	BDOC/DISP RR
122C	BDOC/DISP TR
123	DORM CORRIDOR
124	VESTIBULE
125	DORM
126	DORM
127	DORM
128	DORM
129	DORM
130	DORM
131	PUBLIC RR
132	JAN
133	OFFICER'S WATCH DESK OFFICE
134	DORM
135	DORM
136	DORM
137	DORM
138	DORM
139	DORM
140	DORM
141	DORM
142	DORM
143	DORM
144	DORM
145	DORM
146	DORM
147	DORM
148	ASST. CHIEF / SHIFT SUPERVISOR
149	DORM
150	RR
151	DORM
152	ASST. CHIEF OF FIRE PREVENTION
153	DEPUTY CHIEF'S OFFICE
154	DORM
155	RR
156	DORM
157	FIRE CHIEF'S OFFICE
158	APPARATUS CRASH
159	EQUIP WASH / DISINFECT
160	TR
161	PPE GEAR STORAGE
162	SCBA MAINT. ROOM
163	SCBA COMPRESSOR
164	EMT STOR
165	ELEC
166	APPARATUS BAY STORAGE
167	RESERVE DEPL GEAR STORAGE
168	APPARATUS STRUCTURE
169	HOSE
170	HOSE
171	HOSE

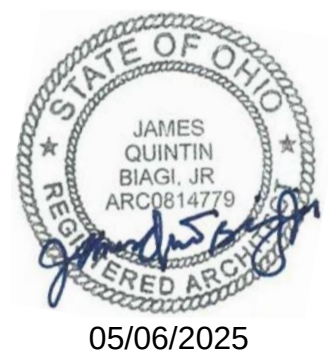

05/06/2025

KEY PLAN

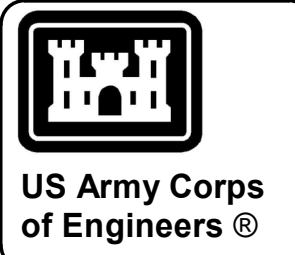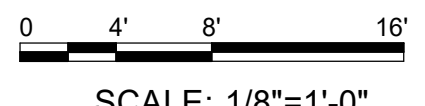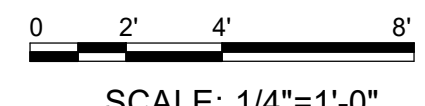

US Army Corps of Engineers®

ISSUE DATE:	26 NOVEMBER 2024
DESIGNED BY:	T. HOUGHAN
DRAWN BY:	T. MOURAD
CHECKED BY:	M. ARMISTEAD
SUBMITTED BY:	M. BERNINGER
SIZE:	ANSI D
AMENDMENT 0004	2
AMENDMENT 0003	1
MARK	
DESCRIPTION	

US ARMY CORPS OF ENGINEERS LOUISVILLE DISTRICT 600 DR. MARTIN LUTHER KING, JR. PLACE LOUISVILLE, KY 40202	ISSUE DATE: 26 NOVEMBER 2024 SOLICITATION NO.: CONTRACT NO.: FY2023
--	---



ZOEL 239001 BASE FIRE STATION YOUNGSTOWN AIR RESERVE STATION, OH
P#: 513392
FURNITURE FLOOR PLAN AREA B

SHEET ID

I-106