


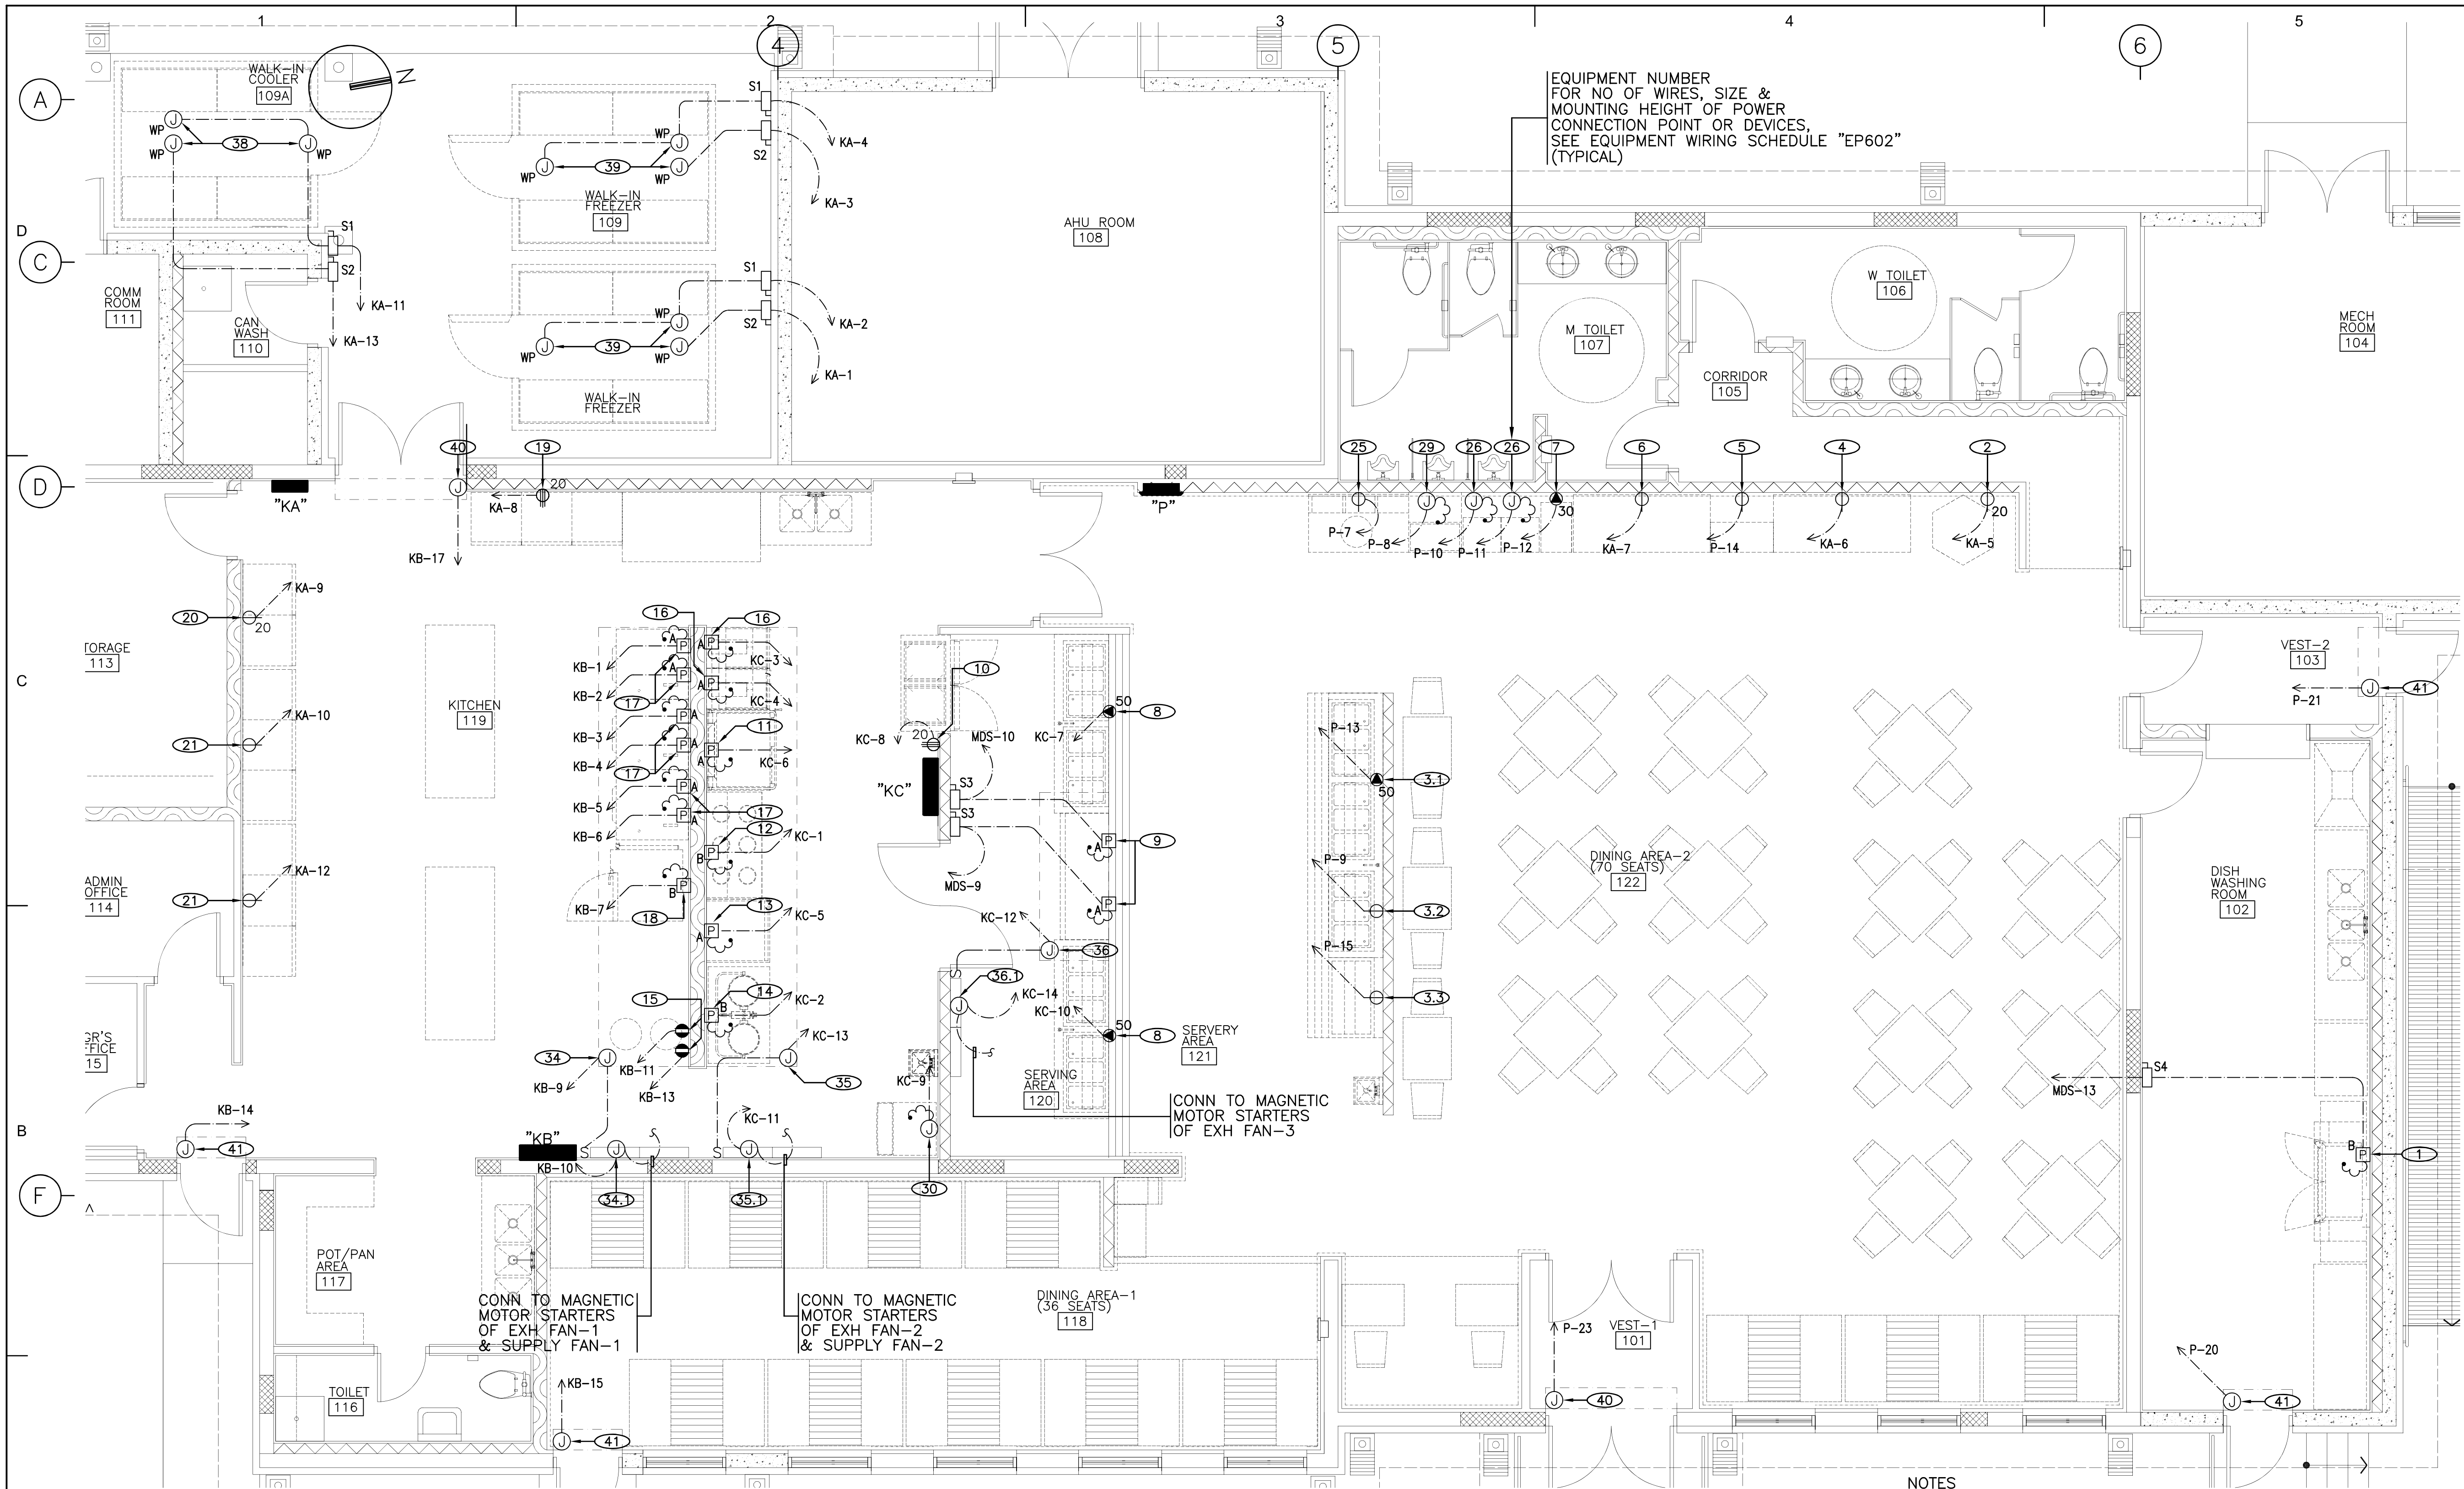

ADDITION LEGEND (THIS SHEET ONLY)

- A
- | | | |
|--|--|---|
| ① (20) : SINGLE RECEPTACLE, 2P-3W-15A(20A)-125V GROUNDING TYPE | ⓘ : GROUND FAULT PROTECTED DUPLEX RECEPTACLE, 2P-3W-15A-125V, GROUNDING TYPE | □ S1 : SAFETY SWITCH, 2PST, 240V, 30A NON-FUSIBLE, NEMA 3R ENCL |
| ⓪ (30/50) : SINGLE RECEPTACLE, 2P-3W-30A(50A)-250V, GROUNDING TYPE | ⓐ : JUNCTION BOX (100x100x50D) W/GASKET AND COVER PLATE | □ S2 : SAFETY SWITCH, 2PST, 240V, 30A W/15A FUSES, NEMA 3R ENCL |
| Ⓜ (20) : SINGLE RECEPTACLE, 3P-4W-20A-250V, GROUNDING TYPE W/PLUG | ⓐA : PULL BOX (150x150x100D) W/GASKET AND COVER PLATE | □ S3 : SAFETY SWITCH, 3PST, 240V, 60A W/60A FUSES, NEMA 4X ENCL |
| | ⓐB : PULL BOX (200x200x150D) W/GASKET AND COVER PLATE | □ S4 : SAFETY SWITCH, 3PST, 240V, 400A W/225A FUSES, NEMA 4X ENCL |

1 NEW KITCHEN PARTIAL POWER PLAN
SCALE : 1/50

0 500 1000 2000
SCALE: 1:50

NOTES

- FOR ABBREVIATION, LEGEND AND GENERAL NOTES, SEE SHEET NO. E-001 & E-002.
- ALL FLEXIBLE CONDUITS BETWEEN EQUIPMENT AND CONNECTION DEVICES SHALL BE PROVIDED WITH THE SAME SIZE OF ITS POWER SUPPLY WIRING.
- CONTRACTOR SHALL CONFIRM THE ELECTRICAL REQUIREMENTS OF THE EQUIPMENT PRIOR TO INSTALLING THE ASSOCIATED CIRCUIT BREAKERS, CONDUIT, WIRING AND MOUNTING HEIGHT OF CONNECTION DEVICE.
- ALL WALL MOUNTED PULL BOX, JUNCTION BOXES, FLEXIBLE CONDUITS AND RECEPTACLES IN KITCHEN, AND DISH WASHING ROOM SHALL BE FLUSH MOUNTED TYPE WATERPROOF UNLESS OTHERWISE INDICATED ON THE DRAWING.

 IMCOM REGIONAL ENGINEER SUPPORT CENTER UNIT 15742, APO AP 96205-5742	
DATE	APPROVED
DATE	DESCRIPTION
DATE	MARK
Reviewed by	Using Agency : Safety Officer : Bldg. & Grounds : Utilities : Fire Prev. & Prot. : Inspection : Others :
Rev.	Date : 25 JUN 10
Scale :	Scale :
Drawn by : J. K. LEE	Checked by : J. K. LEE
Designed by : J. K. LEE	Approved by : J. K. LEE
DEPARTMENT OF THE ARMY INSTALLATION MANAGEMENT AGENCY KOREA REGION OFFICE REGIONAL ENGINEER SUPPORT CENTER UNIT 15742, APO AP 96205-5742	
FY10 OMA FEWR J1-00564-0J CONVERT THE EXISTING BLDG 215 TO DPAC. CAMP WALKER, USAG-DAEGU, KOREA NEW KITCHEN PARTIAL POWER PLAN SHEET IDENTIFICATION NUMBER EP102 Sheet 134 of 149	

CONTRACT(100%)